



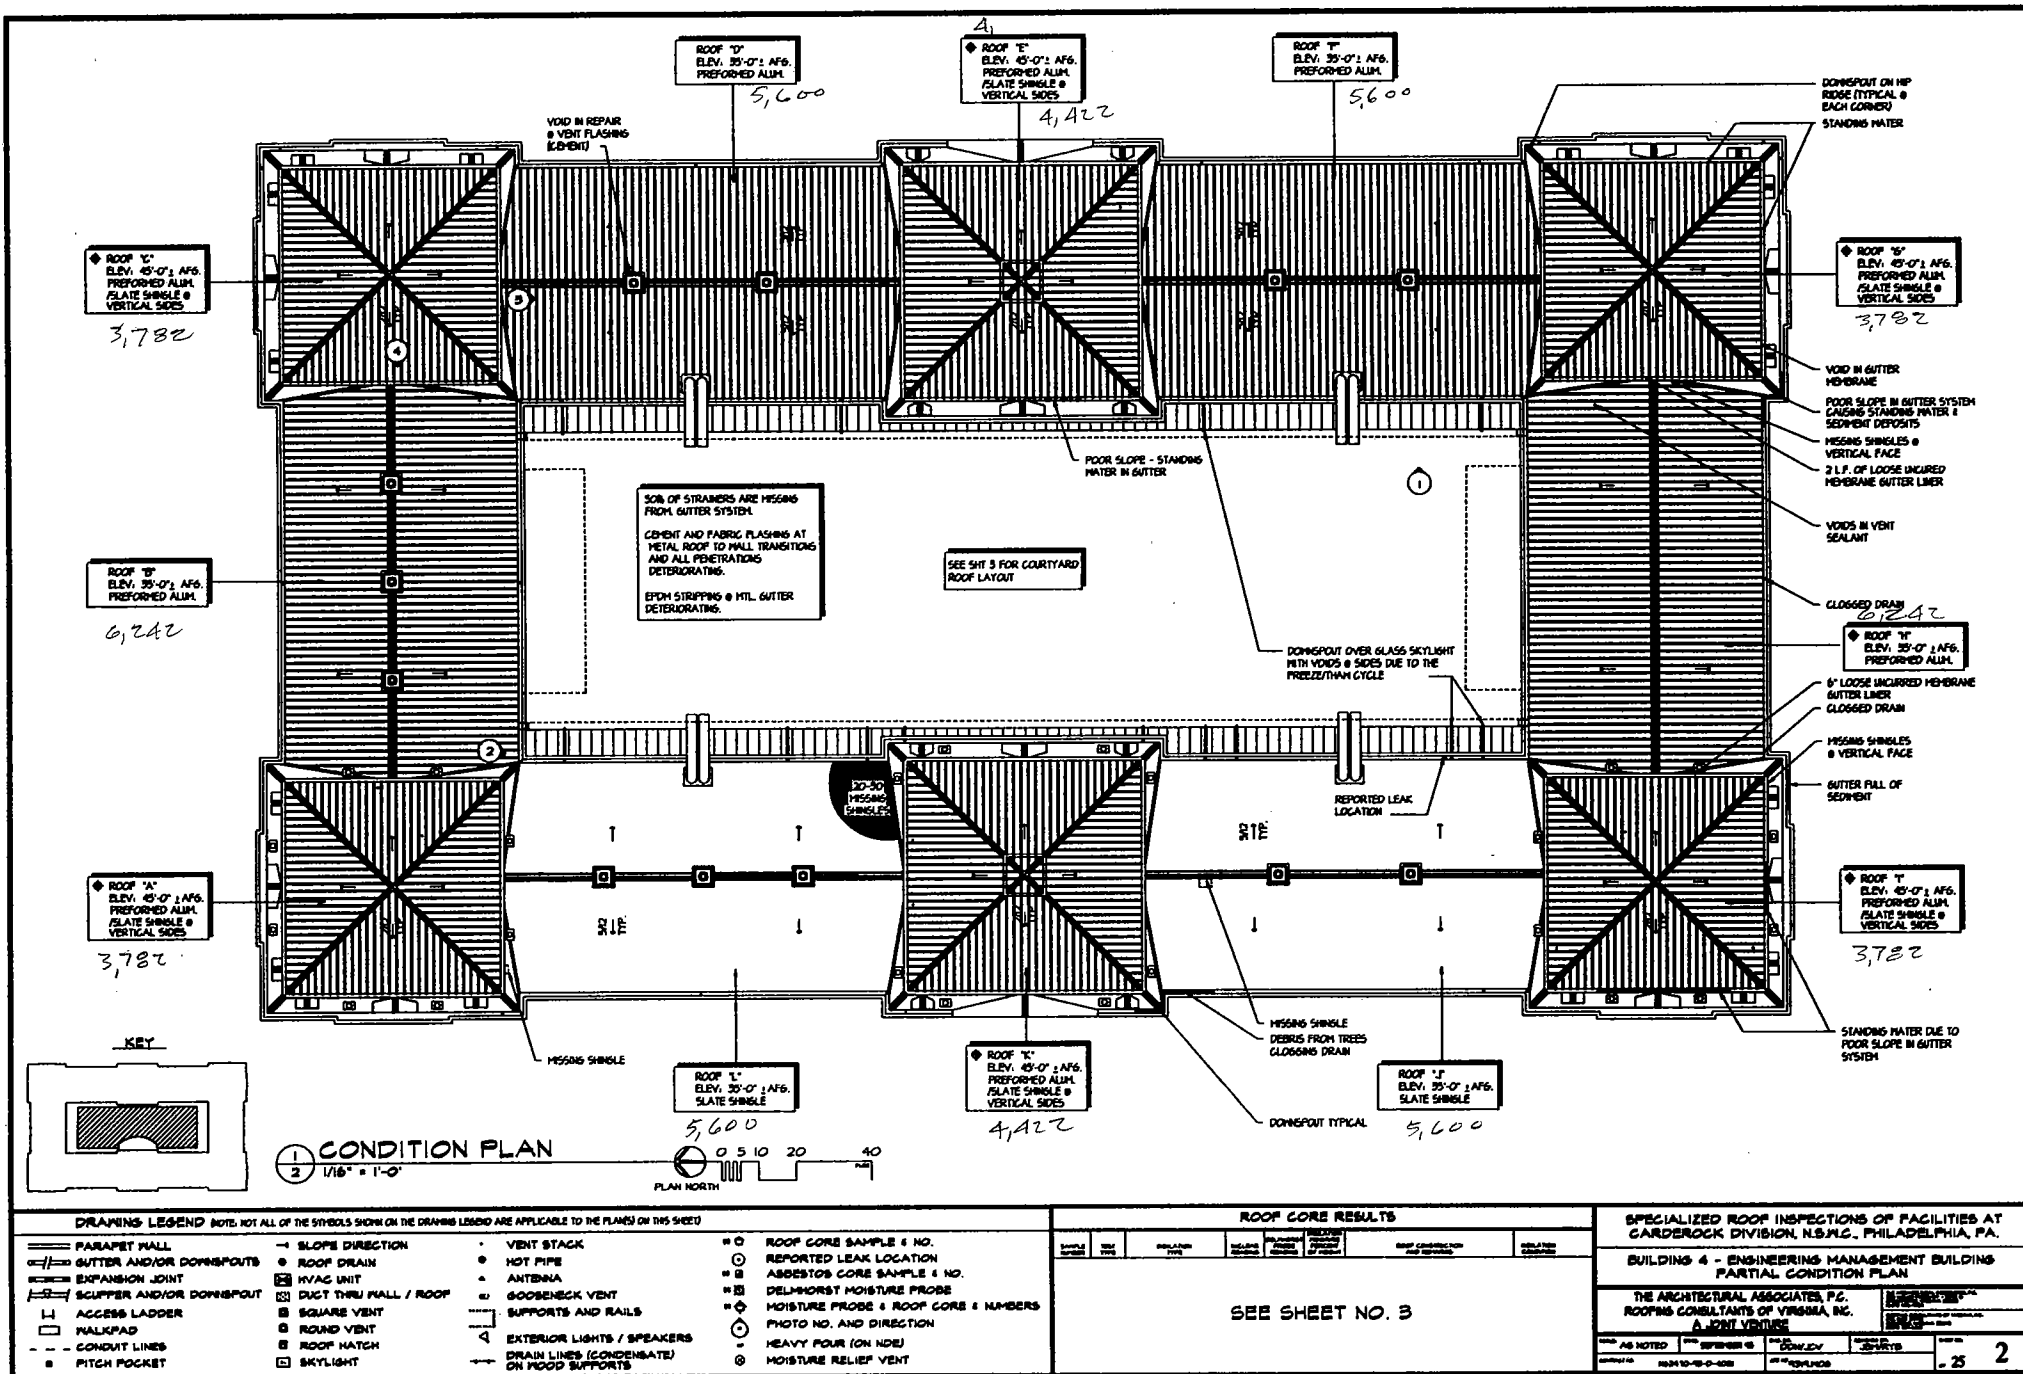

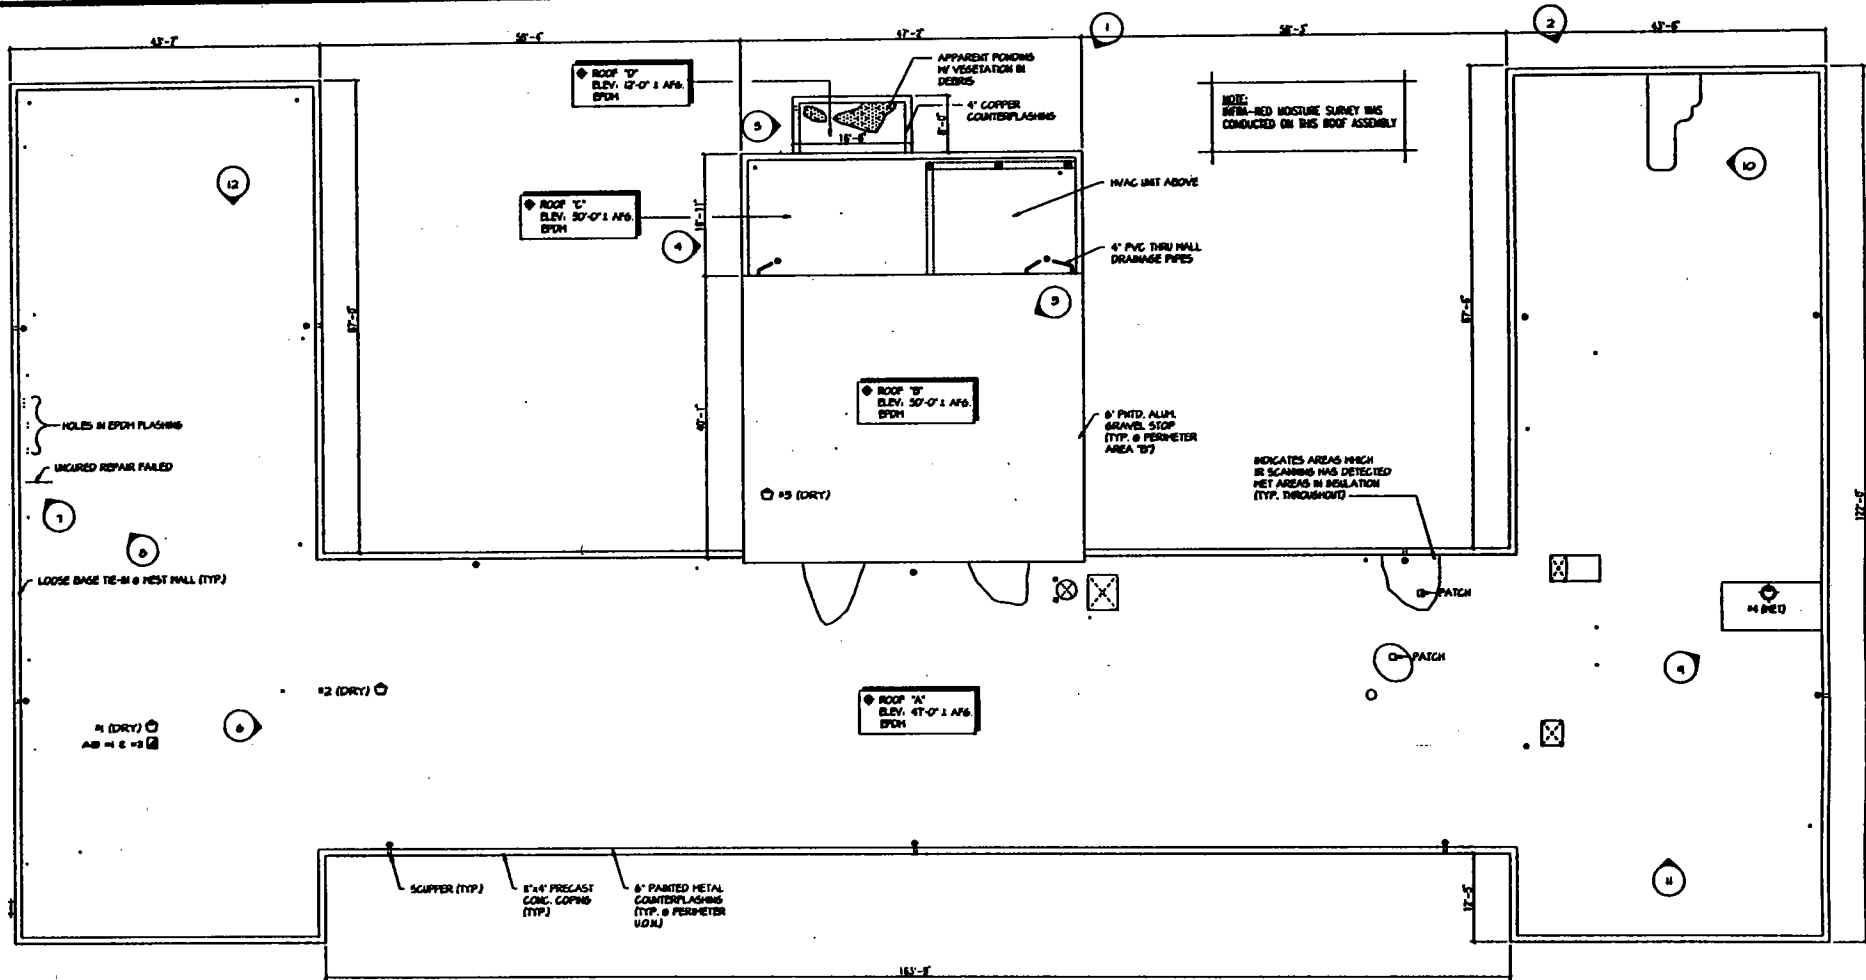


1/8" = 1'-0"
 ACTUAL NORTH

DRAWING LEGEND NOTE: NOT ALL OF THE SYMBOLS SHOWN ON THE DRAWING LEGEND ARE APPLICABLE TO THE PLAN(S) ON THIS SHEET


PARAPET WALL GUTTER AND/OR DOWNSPOUTS EXPANSION JOINT SCUPPER AND/OR DOWNSPOUT ACCESS LADDER WALKPAD CONDUIT LINES PITCH POCKET	SLOPE DIRECTION ROOF DRAIN HVAC UNIT DUCT THRU WALL / ROOF SQUARE VENT ROUND VENT ROOF HATCH SKYLIGHT	VENT STACK HOT PIPE ANTENNA GOOSENECK VENT SUPPORTS AND RAILS EXTERIOR LIGHTS / SPEAKERS DRAIN LINES (CONDENSATE) ON FLOOD SUPPORTS	ROOF CORE SAMPLE # NO. REPORTED LEAK LOCATION ASBESTOS CORE SAMPLE # NO. DEL-HORST MOISTURE PROBE MOISTURE PROBE & ROOF CORE # NUMBERS PHOTO NO. AND DIRECTION HEAVY POUR (ON NEW) MOISTURE RELIEF VENT
--	--	---	--

ROOF CORE RESULTS									
NO.	DATE	TEST	TEST	TEST	TEST	TEST	TEST	TEST	TEST
1	ASBESTOS	2 LAYERS OF ASBESTOS	NO	NO	NO	NO	NO	NO	NO
1	ASBESTOS	2 LAYERS OF ASBESTOS	NO	NO	NO	NO	NO	NO	NO
1	ASBESTOS	2 LAYERS OF ASBESTOS	NO	NO	NO	NO	NO	NO	NO
1	ASBESTOS	2 LAYERS OF ASBESTOS	NO	NO	NO	NO	NO	NO	NO


SPECIALIZED ROOF INSPECTIONS OF FACILITIES AT CARDEROCK DIVISION, N.S./P.C., PHILADELPHIA, PA.			
BUILDING 614 SUBMARINE CASH BARRACKS			
THE ARCHITECTURAL ASSOCIATES, P.C. ROOFING CONSULTANTS OF VIRGINIA, INC. A JOINT VENTURE			
AS NOTED	EXPERIENCE	CONDUCT	RESULTS
25	25	25	25

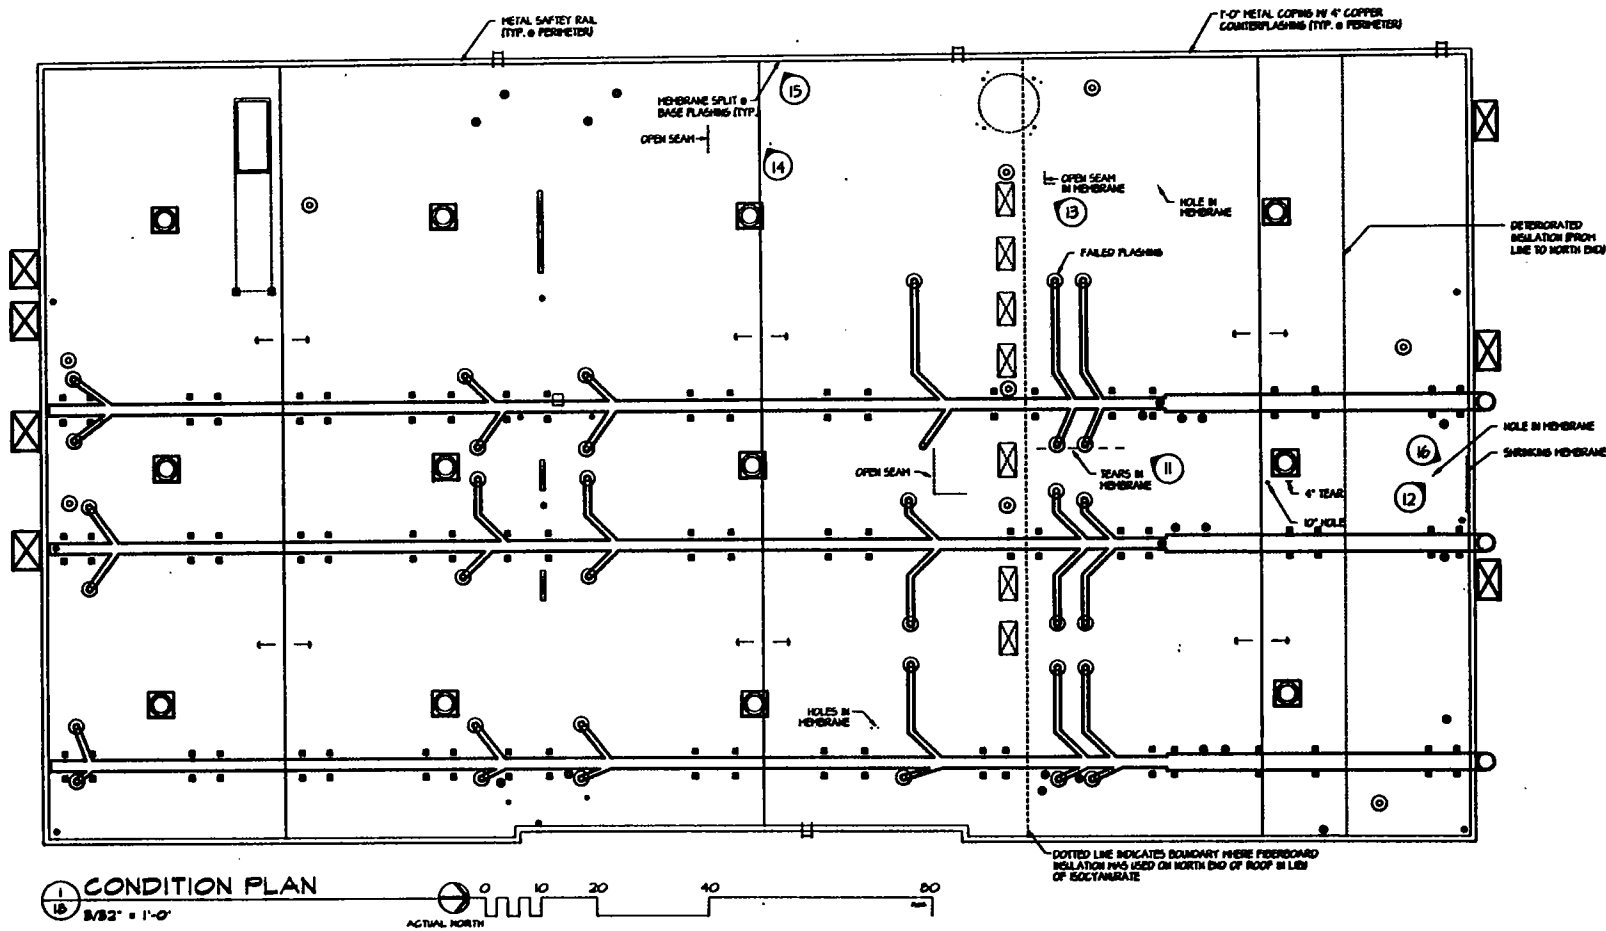

① **CONDITION PLAN**
 3/8" = 1'-0"

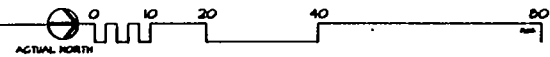

DOTTED LINE INDICATES BOUNDARY WHERE FIBERBOARD INSULATION WAS USED ON NORTH END OF ROOF IN LIEU OF ECCENTRAITE

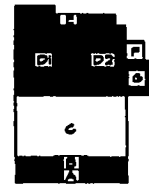


KEY

DRAWING LEGEND: SOME, NOT ALL OF THE SYMBOLS SHOWN ON THE DRAWING LEGEND ARE APPLICABLE TO THE PLAN(S) ON THIS SHEET

- PARAPET WALL - GUTTER AND/OR DOWNSPOUTS - EXPANSION JOINT - SCUPPER AND/OR DOWNSPOUT - ACCESS LADDER - WALKPAD - CONDUIT LINES - PITCH POCKET	- SLOPE DIRECTION - ROOF DRAIN - HVAC UNIT - DUCT THRU WALL / ROOF - SQUARE VENT - ROUND VENT - ROOF HATCH - SKYLIGHT	- VENT STACK - HOT PIPE - ANTENNA - GOOSENECK VENT - SUPPORTS AND RAILS - EXTERIOR LIGHTS / SPEAKERS - DRAIN LINES (CONDENSATE) ON ROOF SUPPORTS	- ROOF CORE SAMPLE & NO. - REPORTED LEAK LOCATION - ASBESTOS CORE SAMPLE & NO. - DELMONEST MOISTURE PROBE - MOISTURE PROBE & ROOF CORE & NUMBERS - PHOTO NO. AND DIRECTION - HEAVY FOUR (ON NOE) - MOISTURE RELIEF VENT
--	--	--	--

ROOF CORE RESULTS									
NO.	DATE	ANALYST	TEST NO.	TEST NO.	TEST NO.	TEST NO.	TEST NO.	TEST NO.	TEST NO.
SEE SHEET NO. 19									

SPECIALIZED ROOF INSPECTIONS OF FACILITIES AT CARDEROCK DIVISION, N.S.M.C., PHILADELPHIA, PA.			
BUILDING 635 - TURBINE TEST LAB CONDITION PLAN			
THE ARCHITECTURAL ASSOCIATES, P.C. ROOFING CONSULTANTS OF VIRGINIA, INC. A JENKINS FIRM		REVISIONS	
NO. AS NOTED	NO. SPECIFIED BY	NO. CORRECTED	NO. REVISED
NO. 10-10-0-001	NO. 10-10-0-001	NO. 10-10-0-001	NO. 10-10-0-001
		25 18	

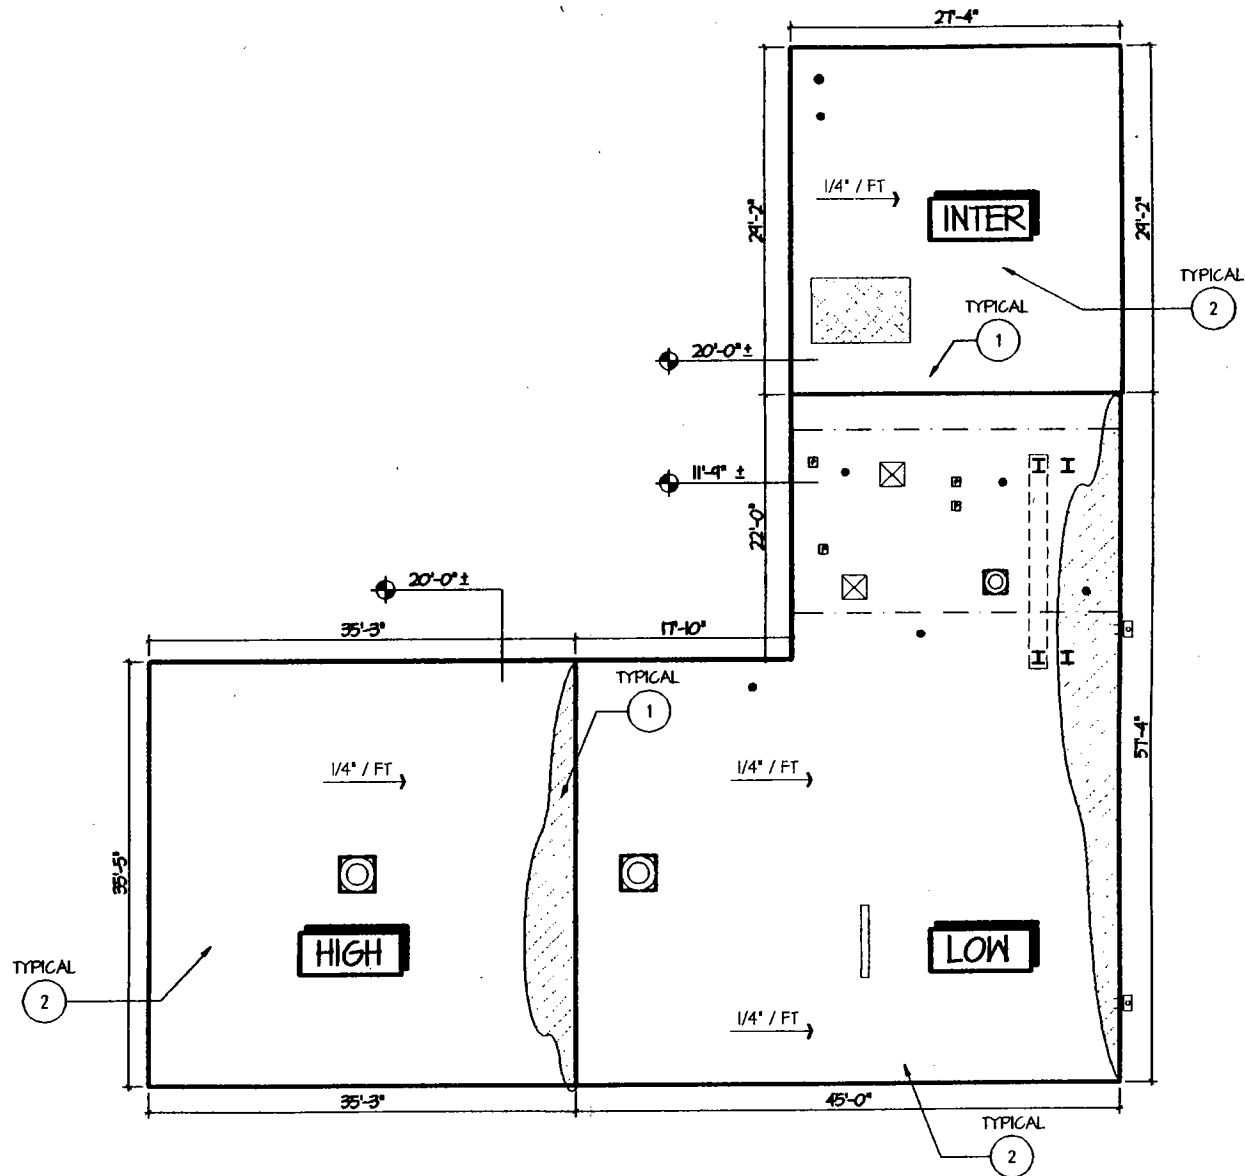

SHEET

43

of 53

PROJECT

SPECIALIZED ROOF INSPECTIONS OF FACILITIES AT CARDEROCK DIVISION,
NAVAL SURFACE WARFARE CENTER, PHILADELPHIA, PA

DRAWING

BUILDING 745 - FIREROOM SCHOOL BOILER REPAIR SHOP


SCALE

NO SCALE

THE ARCHITECTURAL
ASSOCIATES, PC

ROOFING CONSULTANTS
OF VIRGINIA, INC.
A JOINT VENTURE

DATE	SEPT
PROJECT	4319H06
DESIGNED	TAA
DRAWN	TAA
CHECKED	JEM

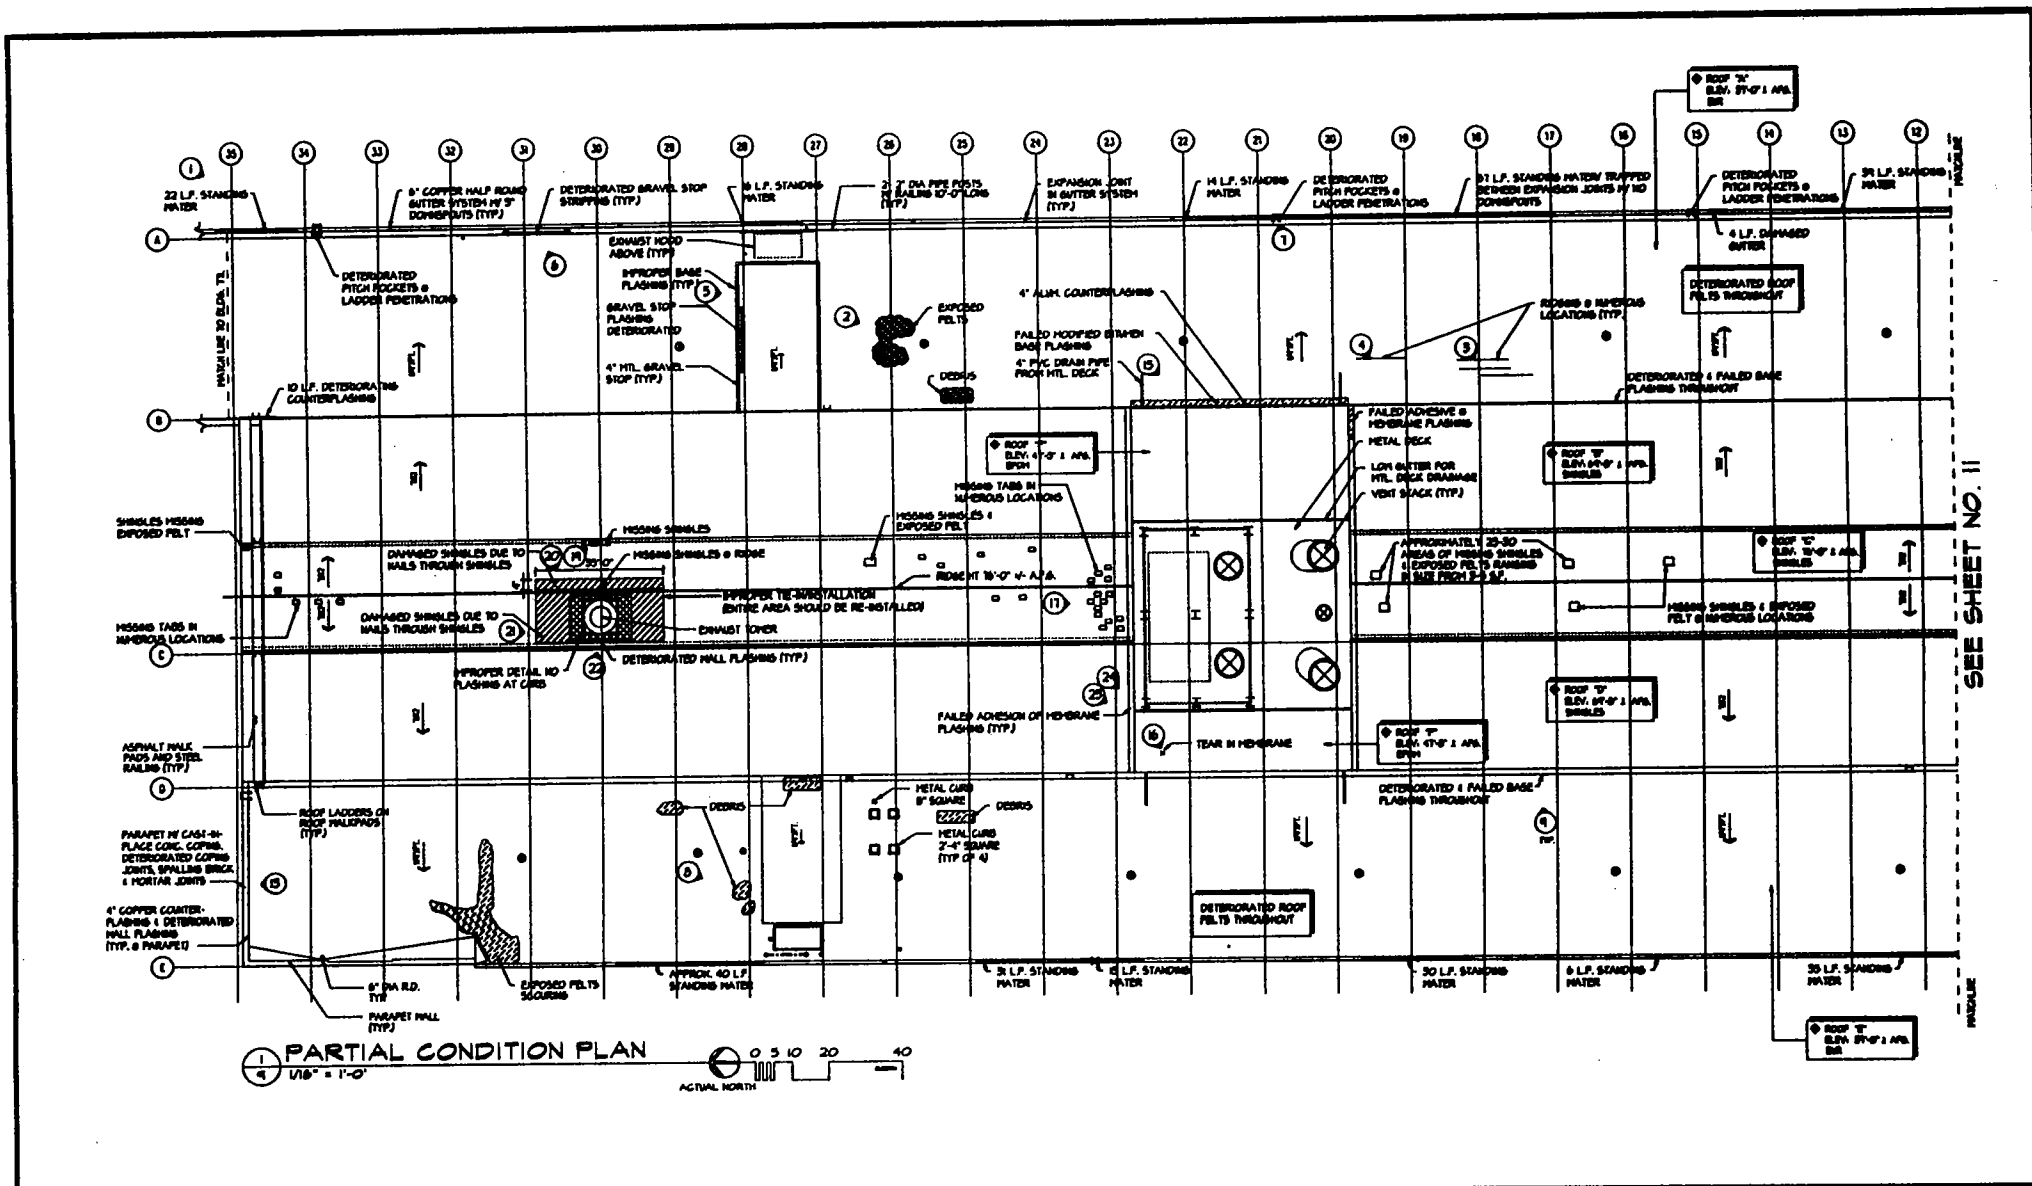


1 PARTIAL CONDITION PLAN
 1/8" = 1'-0"
 ACTUAL NORTH

SEE SHEET NO. 11

DRAWING LEGEND				ROOF CORE RESULTS				SPECIALIZED ROOF INSPECTIONS OF FACILITIES AT CARDEROCK DIVISION, N.S.M.C., PHILADELPHIA, PA.			
NOTE: NOT ALL OF THE SYMBOLS SHOWN ON THE DRAWING LEGEND ARE APPLICABLE TO THE PLAN ON THIS SHEET											
PARAPET WALL	→ SLOPE DIRECTION	• VENT STACK	• ROOF CORE SAMPLE # NO.								
BUTTER AND/OR DOWNSPOUTS	• ROOF DRAIN	• NOT PIPE	• REPORTED LEAK LOCATION								
EXPANSION JOINT	• HYAS UNIT	• ANTENNA	• ASBESTOS CORE SAMPLE # NO.								
SCUPPER AND/OR DOWNSPOUT	• DUST THRU WALL / ROOF	• GOODCHECK VENT	• DELHMONT MOISTURE PROBE								
ACCESS LADDER	• SQUARE VENT	• SUPPORTS AND RAILS	• MOISTURE PROBE # ROOF CORE # NUMBER								
WALKPAD	• ROUND VENT	• EXTERIOR LIGHTS / SPEAKERS	• PHOTO NO. AND DIRECTION								
CONDUIT LINES	• ROOF HATCH	• DRAIN LINES (CONDENSATE) ON ROOF SUPPORTS	• HEAVY FOUR (ON NOE)								
PITCH POCKET	• SKYLIGHT		• MOISTURE RELIEF VENT								

SEE SHEET NO. 10

BUILDING T1E - WAREHOUSE
 PARTIAL PLAN NORTH - CONDITION PLAN
 THE ARCHITECTURAL ASSOCIATES, P.C.
 ROOFING CONSULTANTS OF VIRGINIA, INC.
 A JOINT VENTURE
 PREPARED BY: [Signature]
 DATE: [Date]
 SHEET NO. 9

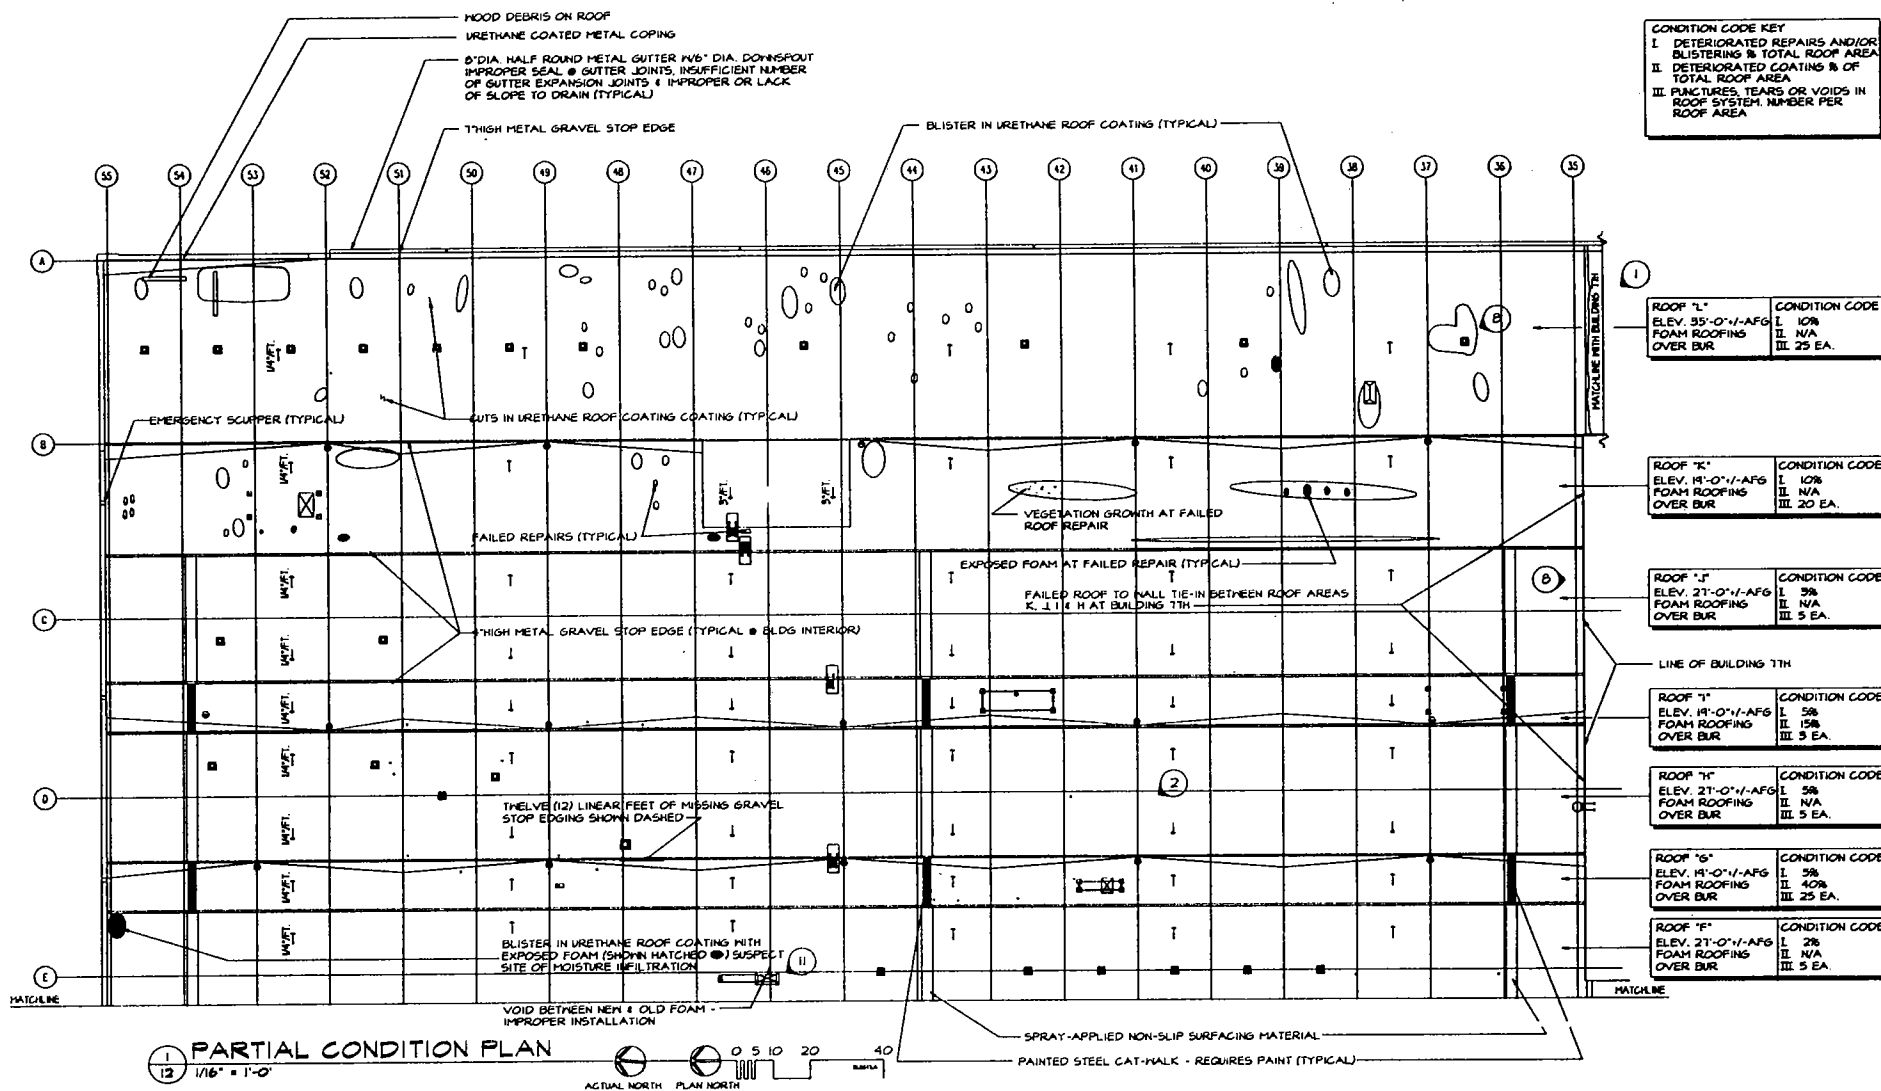

DRAWING LEGEND NOTE: NOT ALL OF THE SYMBOLS SHOWN ON THE DRAWING LEGEND ARE APPLICABLE TO THE PLAN ON THIS SHEET

PARAPET MALL	— SLOPE DIRECTION	VENT STACK	ROOF CORE SAMPLE # NO.
GUTTER AND/OR DOWNSPOUTS	• ROOF DRAIN	• HOT PIPE	REPORTED LEAK LOCATION
EXPANSION JOINT	• HVAC UNIT	• ANTENNA	ASBESTOS CORE SAMPLE # NO.
SCUPPER AND/OR DOWNSPOUT	• DUCT THRU WALL / ROOF	• GOOSENECK VENT	DELINQUENT MOISTURE PROBE
ACCESS LADDER	• SQUARE VENT	• SUPPORTS AND RAILS	MOISTURE PROBE # ROOF CORE # NUMBERS
WALKPAD	• ROUND VENT	• EXTERIOR LIGHTS / SPEAKERS	PHOTO NO. AND DIRECTION
CONDUIT LINES	• ROOF MATCH	• DRAIN LINES (CONDENSATE) ON HOOD SUPPORTS	• HEAVY POUR (ON NOE)
PITCH POCKET	• SKYLIGHT		• MOISTURE RELIEF VENT

ROOF CORE RESULTS

SAMPLE NUMBER	REF TYPE	ROOF CORE TYPE	MOISTURE RELATIVE HUMIDITY	TEMPERATURE	PHOTO NO. AND DIRECTION	ROOF CORE LOCATION AND SERVICES	MOISTURE CONDITION
---------------	----------	----------------	----------------------------	-------------	-------------------------	---------------------------------	--------------------


SEE SHEET NO. 13


SPECIALIZED ROOF INSPECTIONS OF FACILITIES AT CARDEROCK DIVISION, NSWC, PHILADELPHIA, PA.

BUILDING 7TH - ADMINISTRATIVE
PARTIAL PLAN - EAST - CONDITION INSPECTION PLAN

THE ARCHITECTURAL ASSOCIATES, P.C.
ROOFING CONSULTANTS OF VIRGINIA, INC.
A JOINT VENTURE

AS NOTED	SEPTEMBER 15	REVISED	SEPTEMBER 15	DATE	12
----------	--------------	---------	--------------	------	----

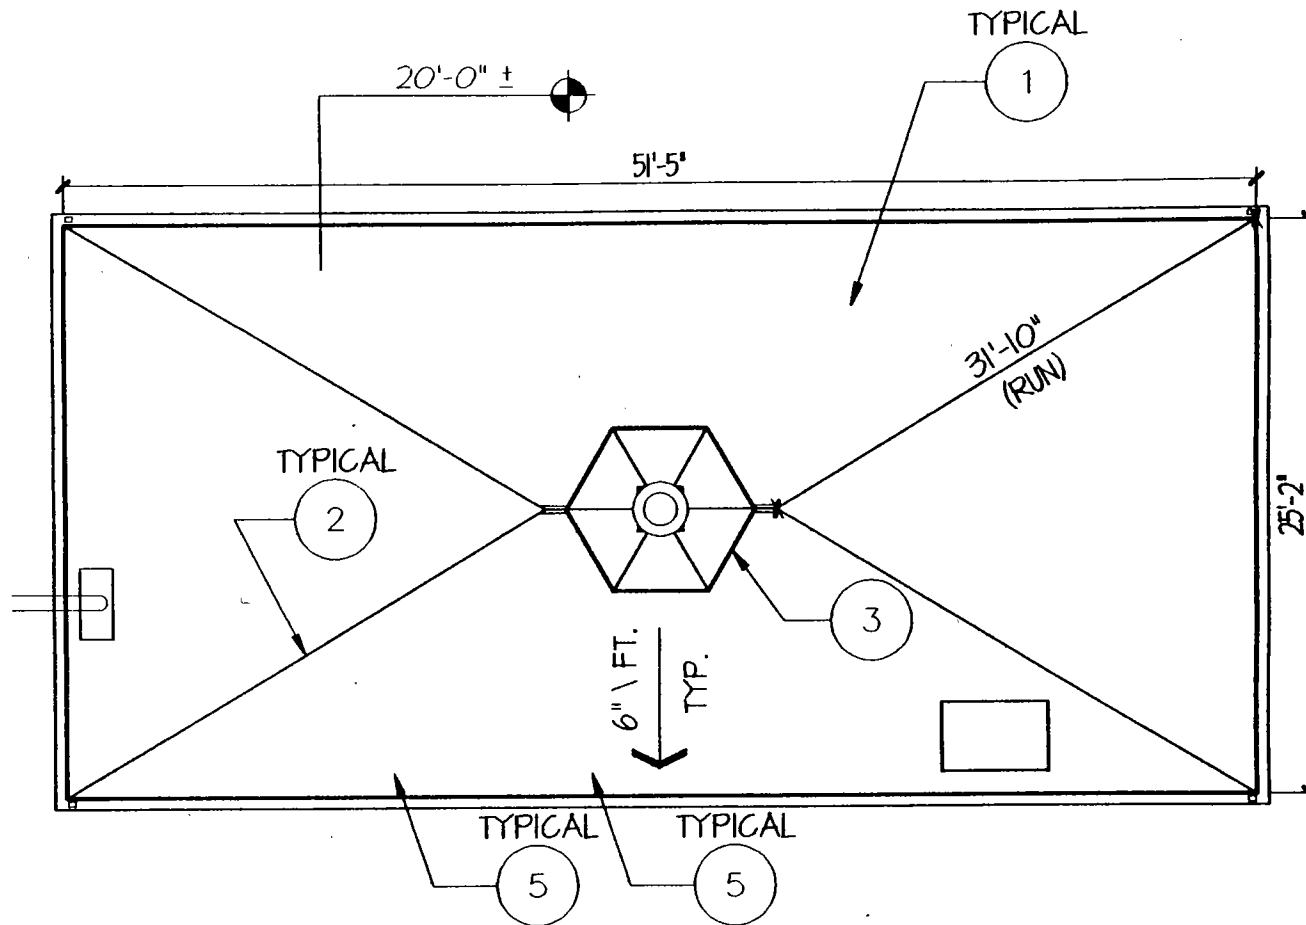

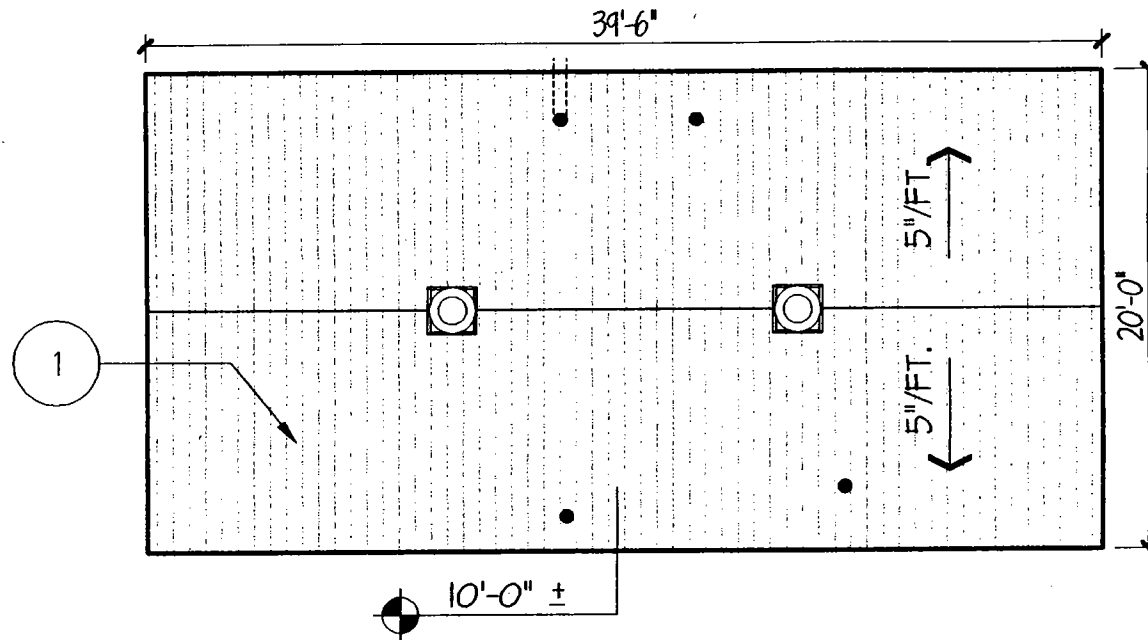

SHEET

18

of 53

PROJECT

SPECIALIZED ROOF INSPECTIONS OF FACILITIES AT CARDEROCK DIVISION,
NAVAL SURFACE WARFARE CENTER, PHILADELPHIA, PA

DRAWING

BUILDING 483 - AIRCRAFT TRUCK FUEL FACILITY

SCALE


NO SCALE

THE ARCHITECTURAL
ASSOCIATES, PC

ROOFING CONSULTANTS
OF VIRGINIA, INC.

A JOINT VENTURE

DATE	SEPT
PROJECT	93191006
DESIGNED	TAA
DRAWN	TAA
CHECKED	JEM

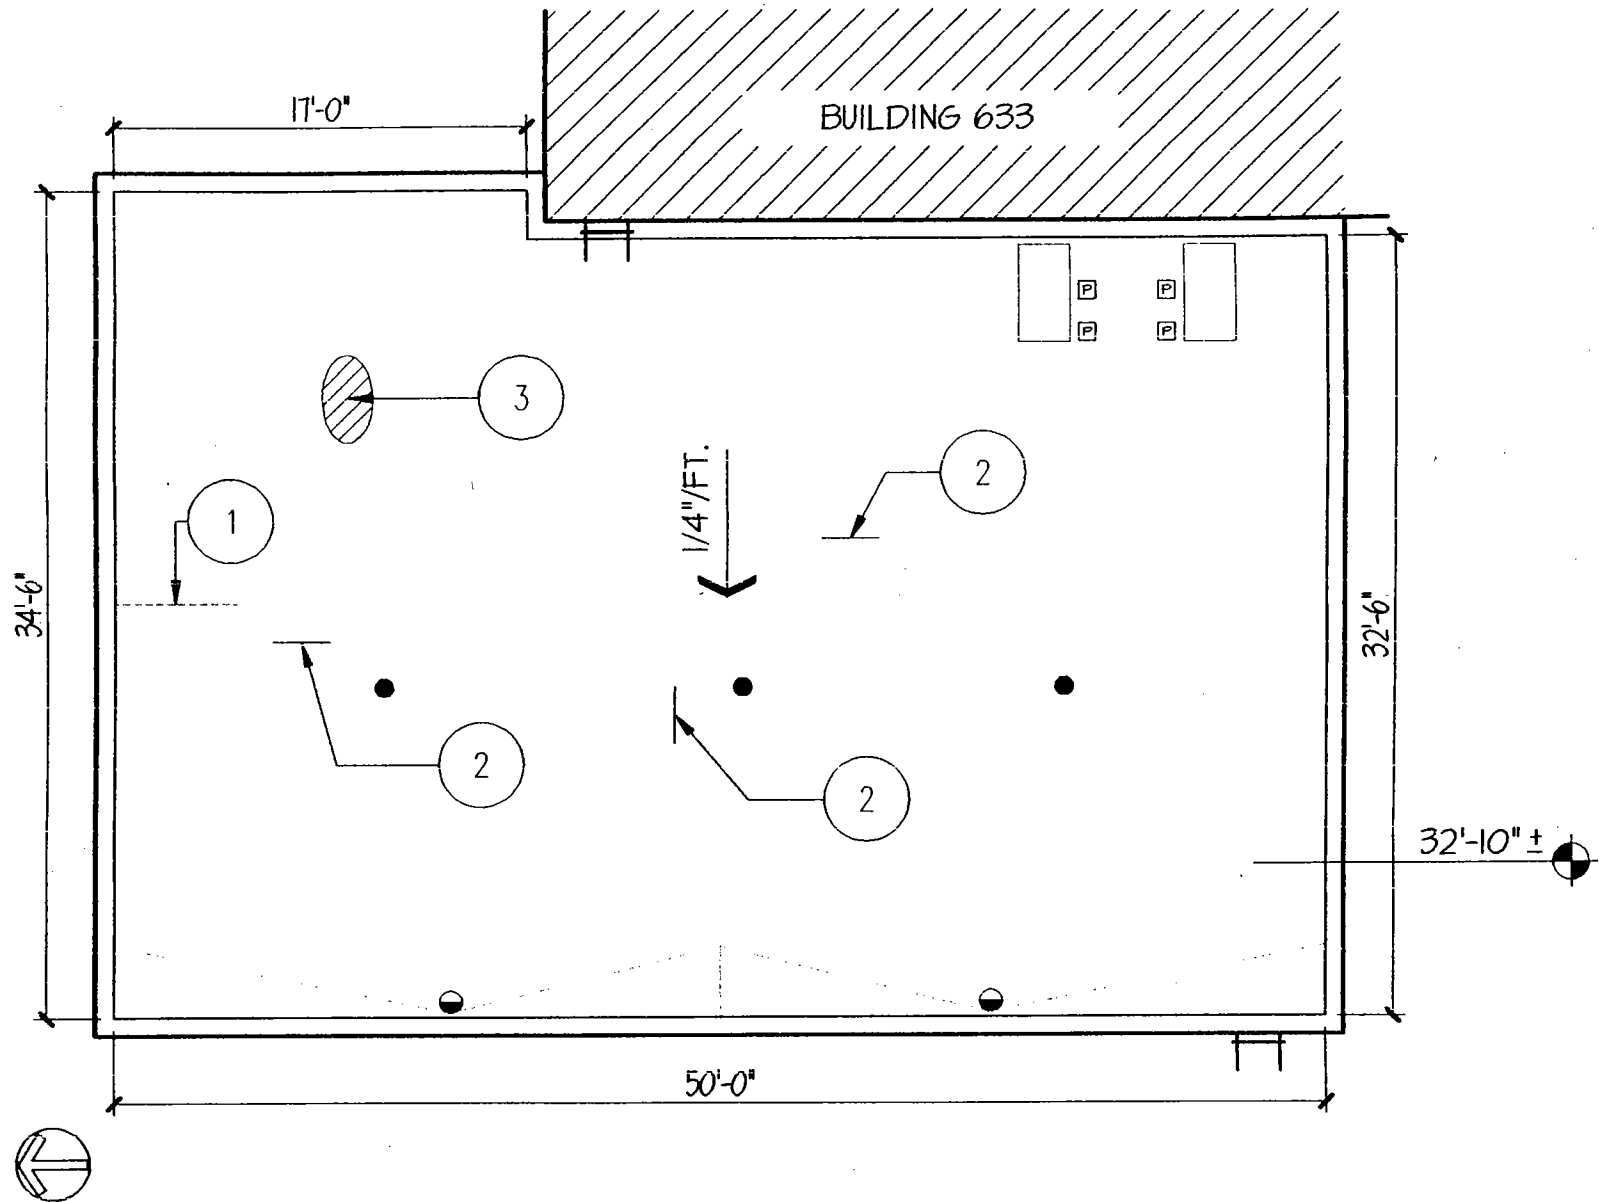

SHEET

37

of 53

PROJECT

SPECIALIZED ROOF INSPECTIONS OF FACILITIES AT CARDEROCK DIVISION,
NAVAL SURFACE WARFARE CENTER, PHILADELPHIA, PA

DRAWING


BUILDING 666 - PUMPHOUSE

SCALE

NO SCALE

THE ARCHITECTURAL
ASSOCIATES, PC
ROOFING CONSULTANTS
OF VIRGINIA, INC.
A JOINT VENTURE

DATE	SEPT
PROJECT	13191406
DESIGNED	TAA
DRAWN	TAA
CHECKED	JEM

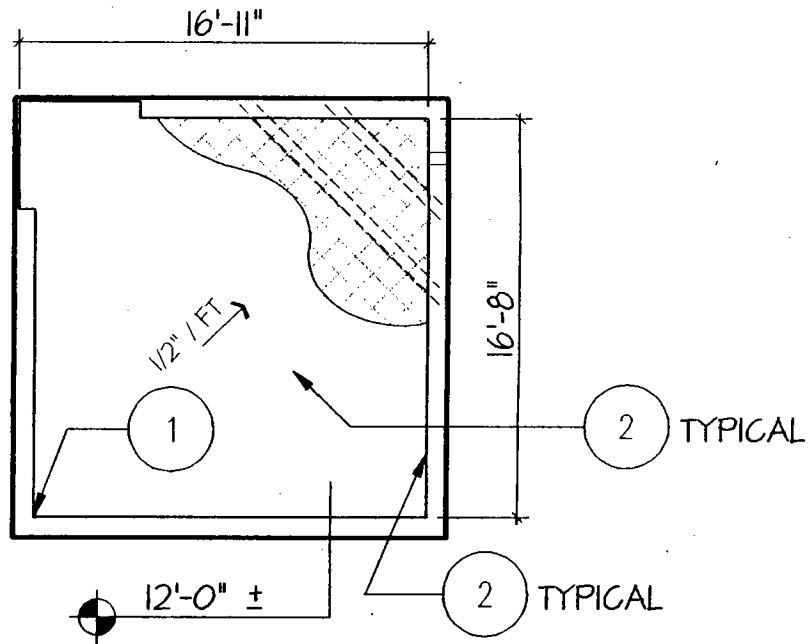

SHEET

43

of 53

PROJECT

SPECIALIZED ROOF INSPECTIONS OF FACILITIES AT CARDEROCK DIVISION,
NAVAL SURFACE WARFARE CENTER, PHILADELPHIA, PA

DRAWING

BUILDING 770 - INSTRUMENT ROOM

SCALE


NO SCALE

THE ARCHITECTURAL
ASSOCIATES, PC

ROOFING CONSULTANTS
OF VIRGINIA, INC.

A JOINT VENTURE

DATE	SEPT
PROJECT	93MPC
DESIGNED	TAA
DRAWN	TAA
CHECKED	JEM

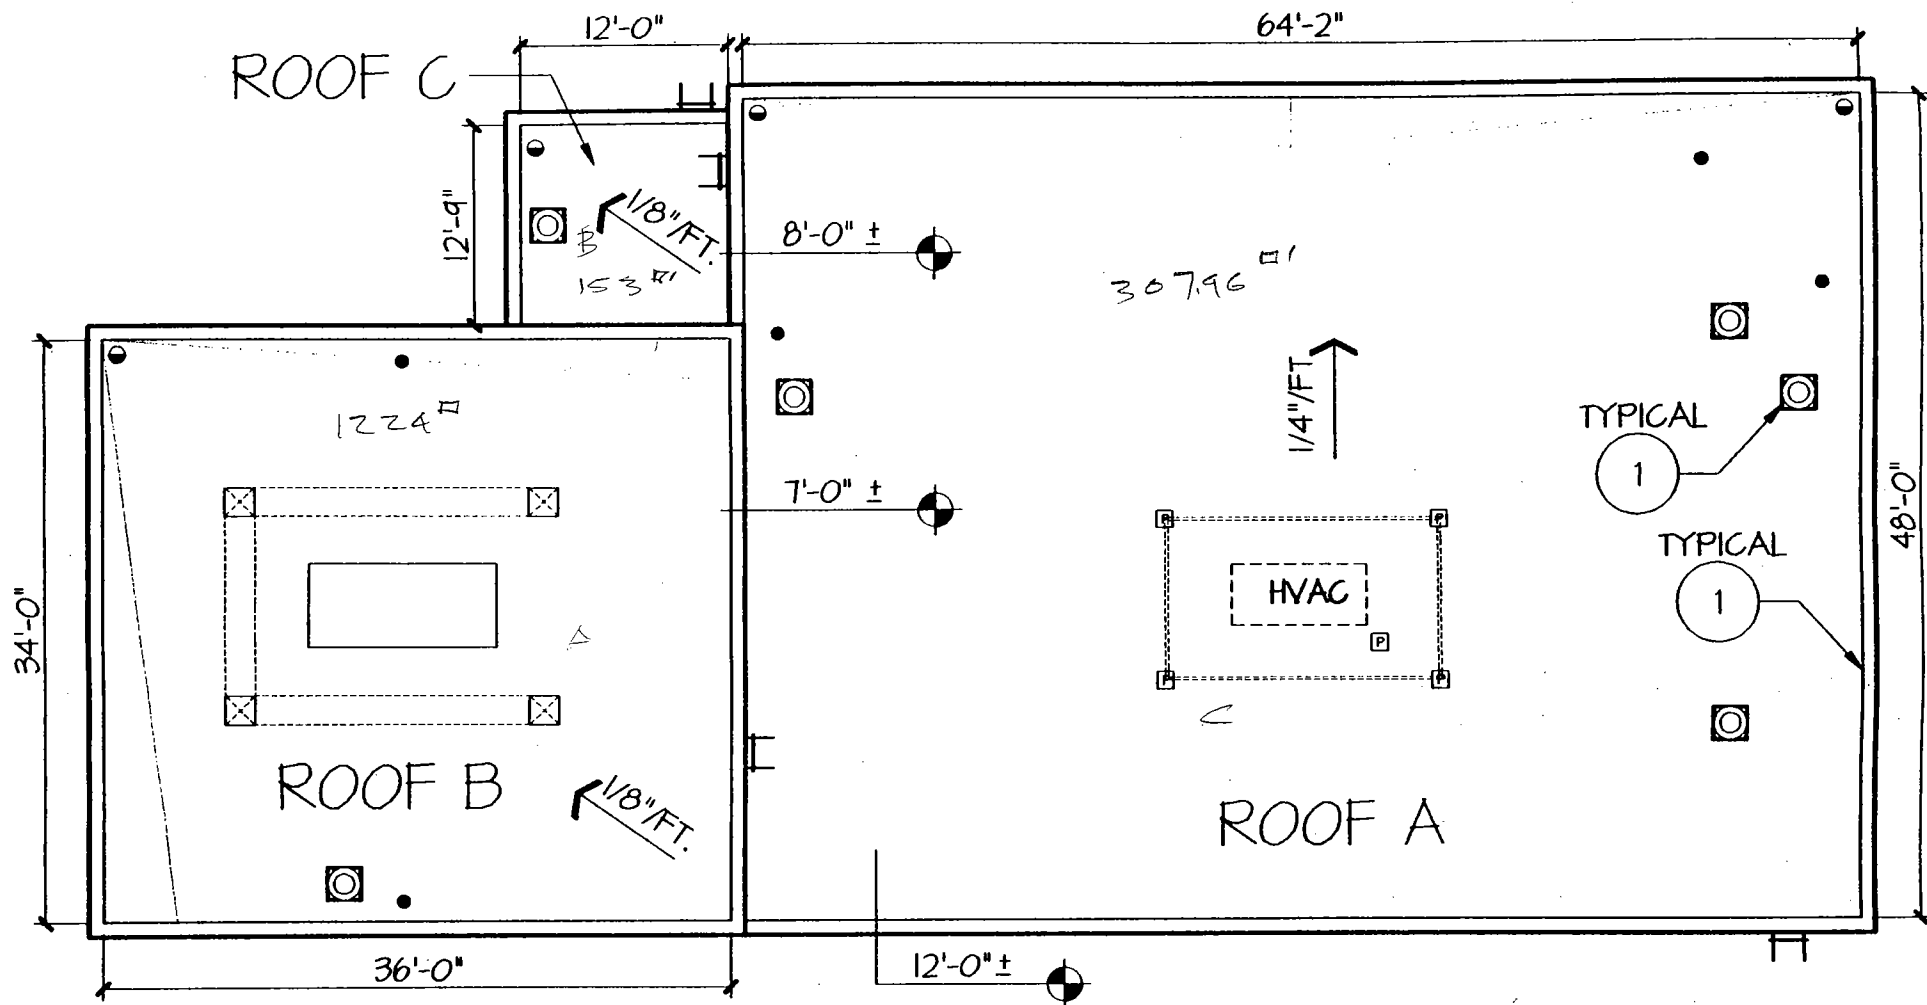

SHEET

17

of 53

PROJECT

SPECIALIZED ROOF INSPECTIONS OF FACILITIES AT CARDEROCK DIVISION,
NAVAL SURFACE WARFARE CENTER, PHILADELPHIA, PA

DRAWING

BUILDING 480 - DENTAL LAB

SCALE

NO SCALE

THE ARCHITECTURAL
ASSOCIATES, PC

ROOFING CONSULTANTS
OF VIRGINIA, INC.

A JOINT VENTURE

DATE

SEPT

PROJECT

43H106

DESIGNED

TAA

DRAWN

TAA

CHECKED

JEM

