
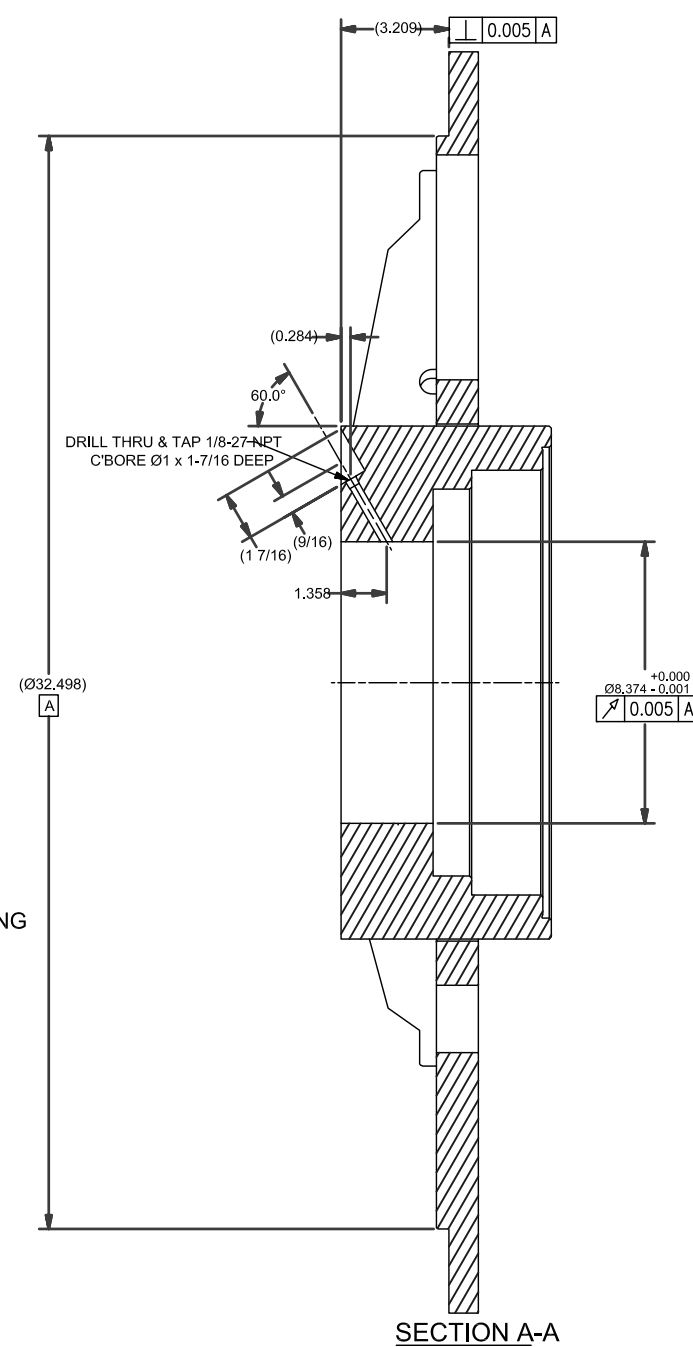


Hole Table		
HOLE	XDIM	YDIM
A	2.188	3.789
A2	2.188	-3.789
A3	1.132	-4.226

- | GENERAL NOTES | |
|---------------|---|
| 1. | REPLACE THERMOWELL IF DAMAGED DURING REMOVAL WITH 10032548-065. |
| 2. | PRIOR TO RE-WELDING; ENSURE THERMOWELL IS RECESSED $\frac{1}{16}$ " MINIMUM FROM BEARING BORE. |
| 3. | SLEEVE HAS A 0.001-0.003 INTERFERENCE FIT WITH END FRAME. PRESS OR SHRINK AS REQUIRED TO ASSEMBLE AS SHOWN. |
| 4. | WHEN INSERTING SLEEVE, SLOT MUST BE ALIGNED WITH $\frac{1}{8}$ NPT HOLE. |
| 5. | HONE AS REQUIRED. |
| 6. | SURFACE FINISH TO BE 125 MICROINCH UNLESS OTHERWISE NOTED. |

REVISIONS						
REV	SH	ZONE	ITEM	DESCRIPTION	DATE	APPL SIG & ORG
—	—	—	—	INITIAL RELEASE. ACTIVITY 57441.	10/18/23	M. CHES/s/ SFLC-ESD- NAME-MPMS

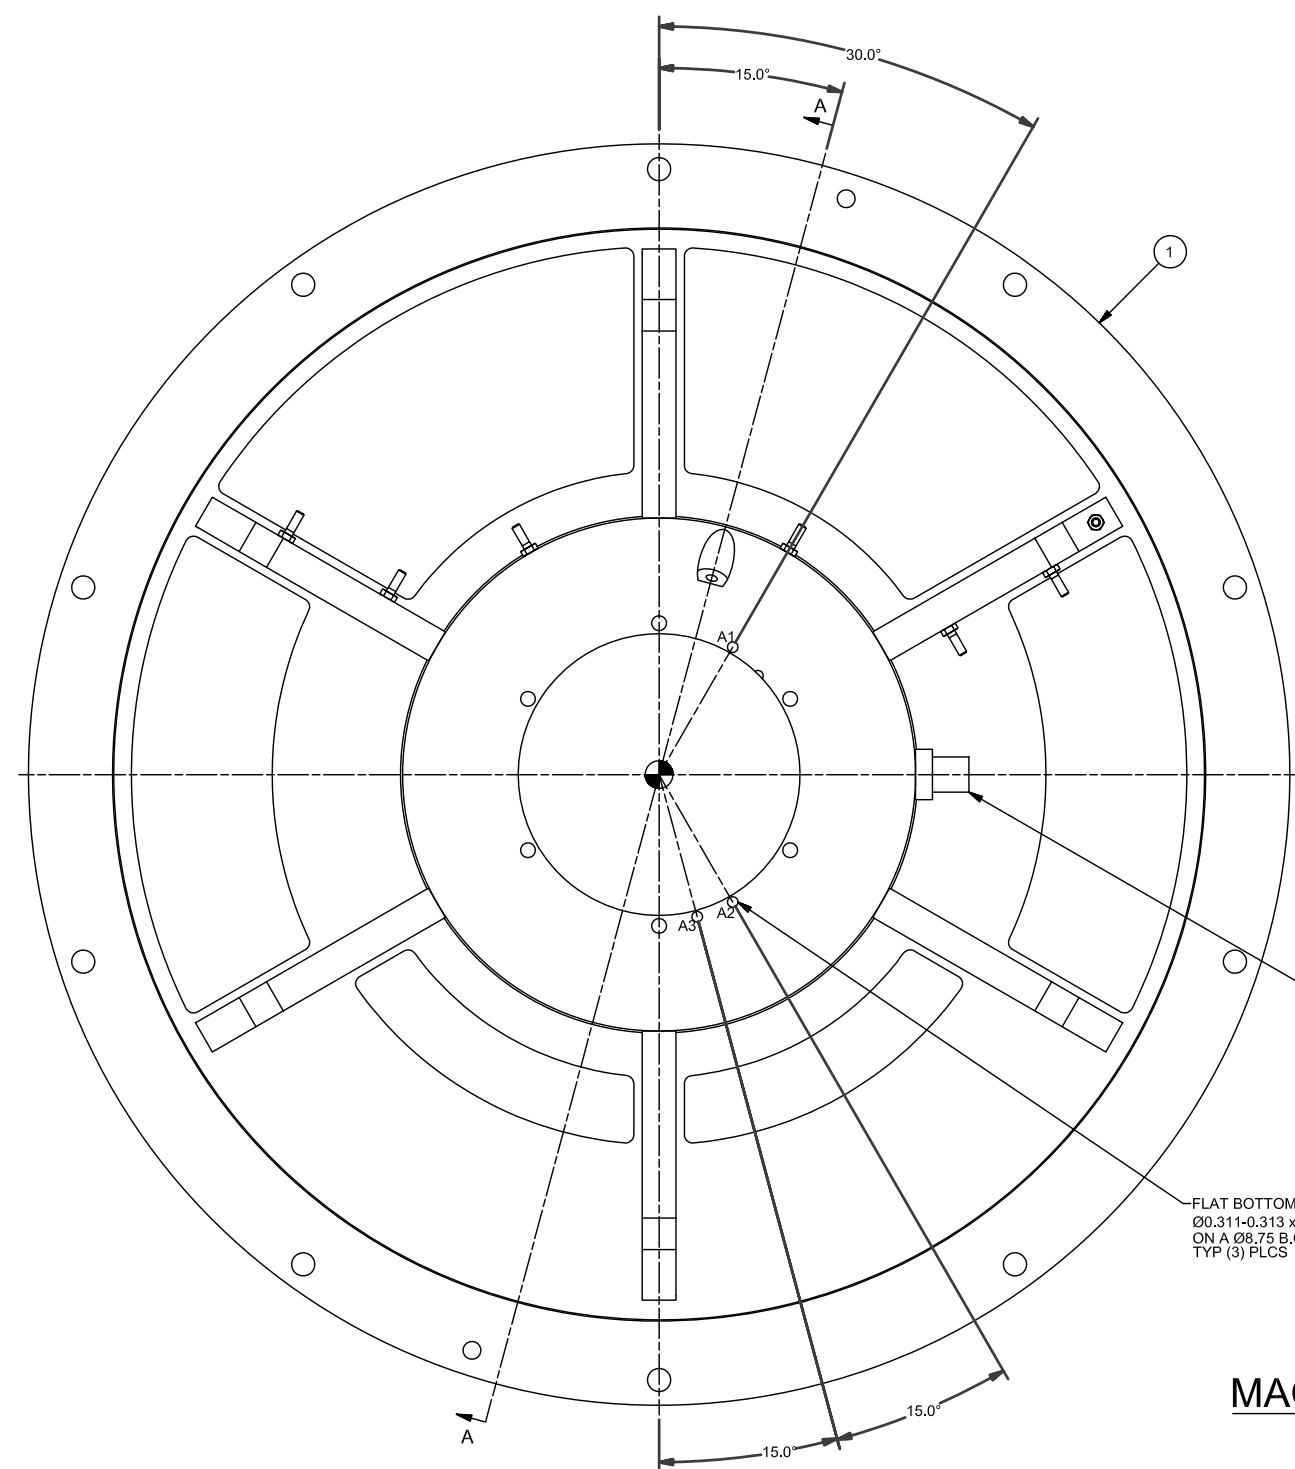

4		
3		
2		
1	SSDG MODEL 3512B MISCELLANEOUS VENDOR MANUALS	7119-311-B
NO.	TITLE	DRAWING NO.

REFERENCE PLANS

SPECIAL NOTATIONS

STINFO DESIGNATION

DISTRIBUTION STATEMENT D: DISTRIBUTION AUTHORIZED TO DHS/CG/DOD AND THEIR CONTRACTORS FOR ADMINISTRATIVE AND OPERATIONAL PURPOSES; 10/18/2023. OTHER REQUESTS SHALL BE REFERRED TO COMMANDING OFFICER, USCG SFLC ESD TMB, 2401 HAWKINS POINT ROAD, MAIL STOP 25/STINFO PROJECT MANAGER, BALTIMORE, MD 21226-5000.

WARNING: THIS DOCUMENT CONTAINS TECHNICAL DATA WHOSE EXPORT IS RESTRICTED BY THE ARMS EXPORT-CONTROL ACT (TITLE 22, U.S.C. SEC 2751, ET. SEQ.) OR THE EXPORT ADMINISTRATION ACT OF 1979, AS AMENDED, TITLE 50, U.S.C. APP 2401 ET. SEQ. VIOLATIONS OF THESE EXPORT LAWS ARE SUBJECT TO SEVERE CRIMINAL PENALTIES.

DESTRUCTION NOTICE: FOR UNCLASSIFIED, LIMITED DOCUMENTS, DESTROY BY ANY METHOD THAT WILL PREVENT DISCLOSURE OF CONTENTS OR RECONSTRUCTION OF THE DOCUMENT.

USCG SFLC ESD 707 E. ORDNANCE ROAD BALTIMORE, MD 21226 PHONE: (410) 762-6700 CONTRACT/PO NO.	UNITED STATES COAST GUARD			WASHINGTON, D.C. 20593
	OFFICE OF NAVAL ENGINEERING			
	418 FT		WMSL	
	SSDG GENERATOR BEARING END FRAME, NON-DRIVE END MACHINING			
	SELECTED RECORD DRAWING			
DESIGNED: M. CHES /s/	10/18/23	UPDATE REQUIRED FOR ALL AUTHORIZED CONFIGURATION CHANGES.		
DRAWN: M. CHES/s/	10/18/23	SIZE	CAGE CODE	USCG DRAWING NO.
CHECKED: T. GARLAND /s/	10/18/23	C	81340	750-WMSL 310 507
APPROVED: M. CHES /s/	10/18/23	REV		
USCG APPROVAL	10/18/23	—		
T. GARLAND /s/				
ESS TA		SCALE: AS NOTED		SHEET: 1 OF 2

Parts List				
ITEM	QTY	UOM	PART NUMBER	MATERIAL/DESCRIPTION
1	1	EA	10008275-001	END FRAME, NON-DRIVE END WELD/MACHINING
2	1	EA	11370466-001	SLEEVE, BEARING NON-DRIVE END

WEIGHT CONTROL								
WEIGHT GROUP	DESCRIPTION	WEIGHT (LBS)	VCG REF BL	LCG REF (SEE NOTE)	F/A	TCG REF CL	P/S	
SWBS	END FRAME, NDE	377	0.0	0.0	F/A	0.0	P/S	

MACHINING TOLERANCES UNLESS OTHERWISE SPECIFIED		
DECIMAL PLACES	TOLERANCE	ANGLES $\pm 0^{\circ} 30''$
ONE 0.0	± 0.060	WELD BEVELS AND CHAMFERS $\pm 2^{\circ} 30''$
TWO 0.00	± 0.020	THREADS UN-2A, 2B
THREE 0.000	± 0.005	FILLETS 0.04R MAX
		BREAK CORNERS 0.02-0.04 X 45
		REMOVE ALL BURRS

WMSL	750-758
ASSET CLASS	HULLS
APPLICABILITY	

