

D



2

3

4

- D

C




KEYED NOTES 

NOTAS DE REFERENCIA

- KEYED NOTES** 
- NOTAS DE REFERENCIA*



- GRAPHIC SCALE(S):**
ESCALA(S) GRÁFICA(S):

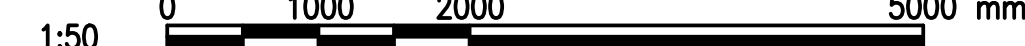NAMEAC METRIC DRAWFORM REVISION: 03 AUGUST 2018




KEYED NOTES
NOTAS DE REFERENCIA 

- GENERAL NOTES**
NOTAS GENERALES

- PLAN
NORTH

GRAPHIC SCALE(S):
ESCALA(S) GRÁFICA(S):

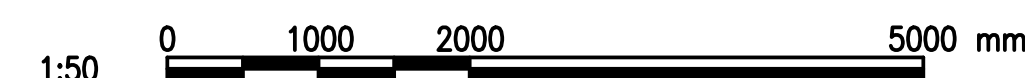


FILE NAME: G:\21 Jobs\21-015 FY 23 MILCON P-919 Bulk Tanks - Rota\CAD\VA-403 BUILDING ELEVATIONS - PUMP VAULTS.dwg LAYOUT NAME: a-403 PLOTTED: Tuesday, June 25, 2024 - 8:30am USER: okdgm

D


C

B

A

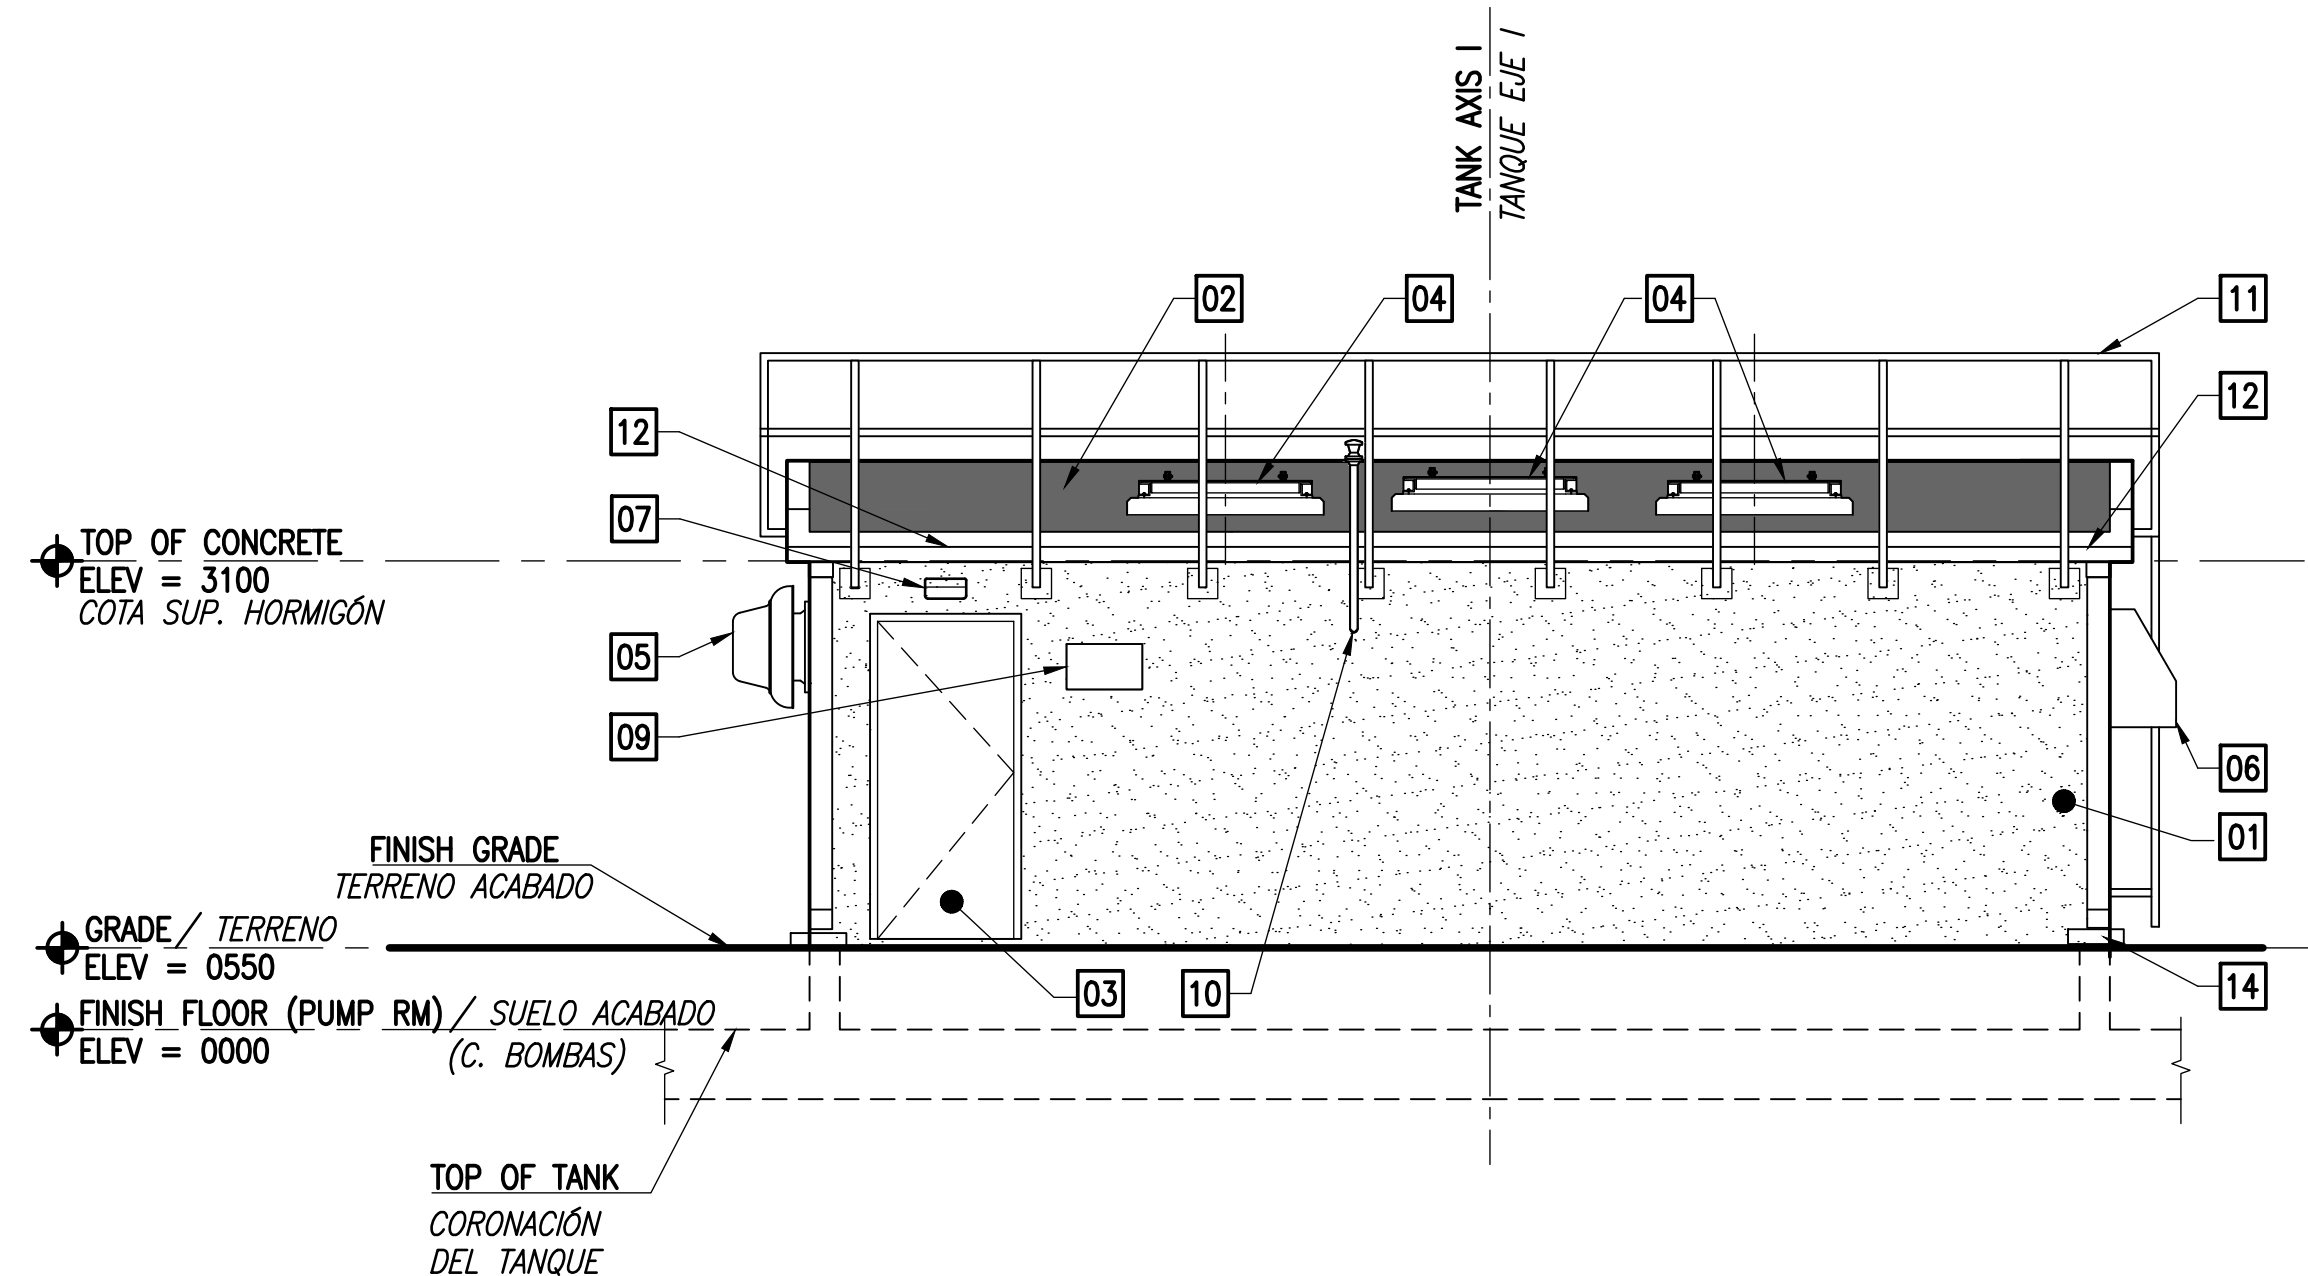

C1 ELEVATION PUMP VAULT / ALZADO CÁMARA DE BOMBAS
SCALE: 1:50

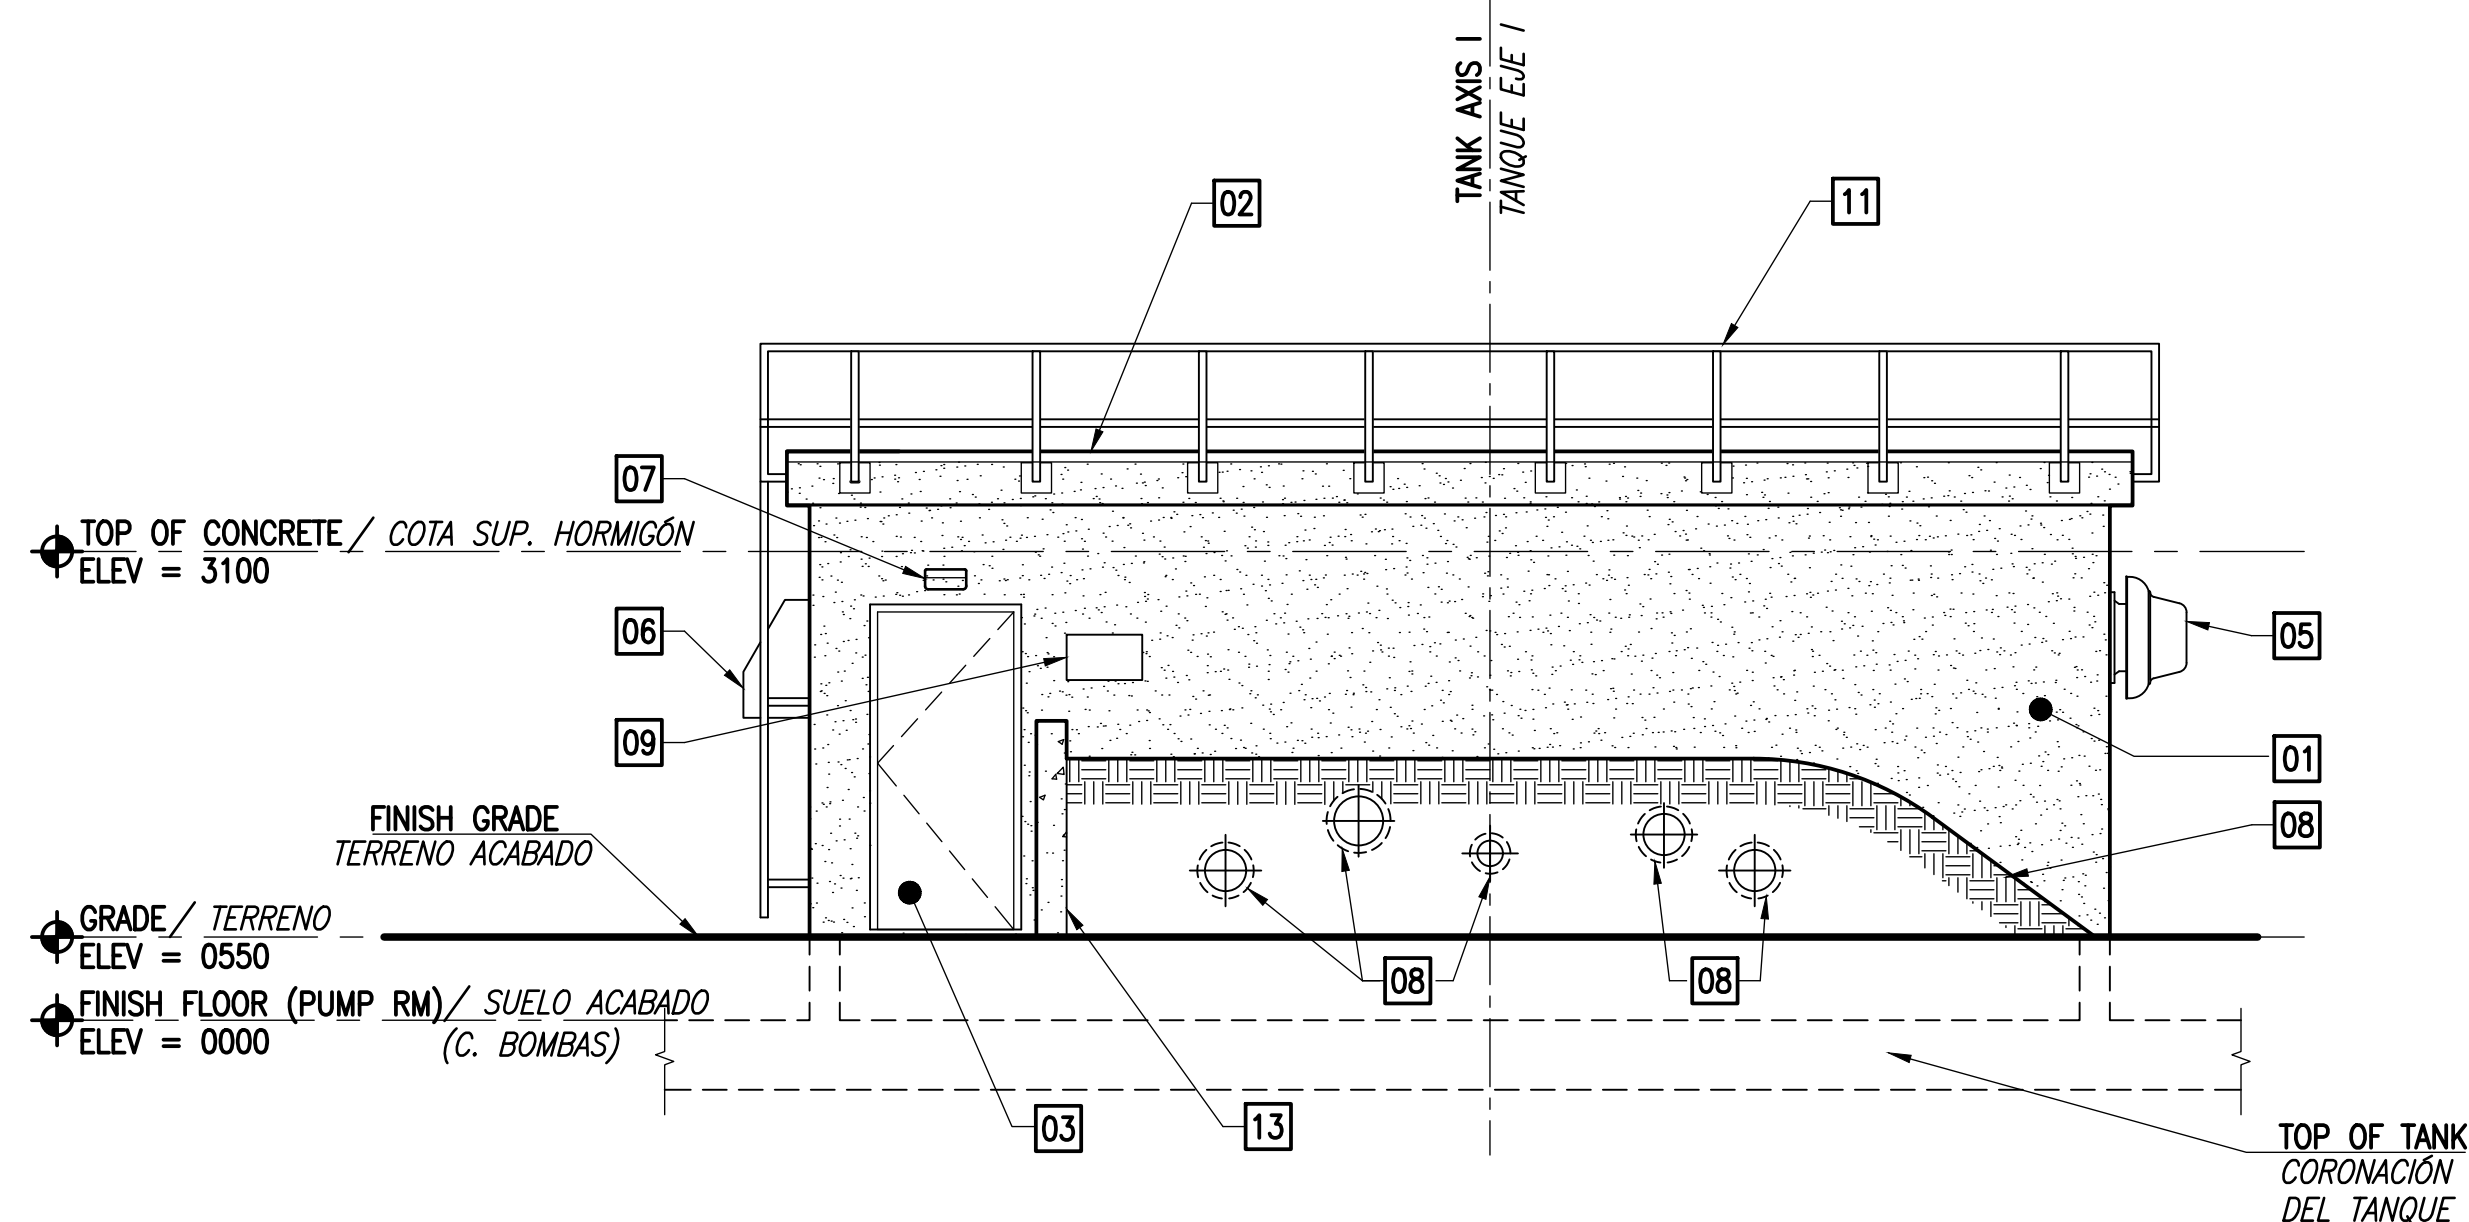


B1 ELEVATION PUMP VAULT / ALZADO CÁMARA DE BOMBAS
SCALE: 1:50


KEYED NOTES / NOTAS DE REFERENCIA

- 01 CONCRETE WALL, STUCCO, PAINTED 200mm THICK - SEE FLOOR PLAN.
01 MURO DE HORMIGÓN, ENFOSCADO, PINTADO DE 200mm DE ESPESOR - VER PLANTA.
- 02 FLUID-APPLIED ELASTOMERIC ROOFING, 3% SLOPE.
02 SISTEMA DE CUBIERTA ELASTOMÉRICA DE APLICACIÓN FLUIDA, PENDIENTE 3%.
- 03 STEEL PLATE SPLINTER DOORS (TYP).
03 PUERTAS ABATIBLES DE CHAPA DE ACERO (TIP).
- 04 ROOF HATCH FOR PUMPS. CENTER HATCH OVER PUMP LOCATIONS.
04 TRAMPILLA EN CUBIERTA PARA BOMBAS. CENTRAR TRAMPILLA SOBRE LAS UBICACIONES DE LAS BOMBAS.
- 05 EXHAUST FAN - SEE MECHANICAL DRAWINGS.
05 EXTRACTOR- VER PLANOS DE MECÁNICA.
- 06 WEATHERPROOF WALL LOUVER WITH STAINLESS STEEL HOOD & SECURITY GRILLE - SEE A4/A-601 AND MECHANICAL DRAWINGS.
06 REJILLA EN PARED RESISTENTE A INTEMPERIE CON CAPERUZA DE ACERO INOXIDABLE Y REJA DE SEGURIDAD - VER A4/A-601 Y PLANOS DE MECÁNICA.
- 07 WALL MOUNTED LIGHT FIXTURE CENTERED OVER DOORS - SEE ELECTRICAL DRAWINGS.
07 LUMINARIA MONTADA EN PARED CENTRADA SOBRE LAS PUERTAS - VER PLANOS ELÉCTRICOS.
- 08 PIPE PENETRATIONS BEYOND EARTH BERM - SEE POL DRAWINGS FOR QUANTITY & LOCATIONS.
08 PENETRACIONES DE TUBERÍA DETRÁS DE LA BERMA DE TIERRA - VER PLANOS POL PARA CANTIDAD Y POSICIONES.

- 09 BUILDING SIGN - PER BASE STANDARDS.
09 SEÑAL DEL EDIFICIO - SEGÚN LAS NORMAS DE LA BASE.
- 10 PIPE VENT PENETRATIONS - SEE POL DRAWINGS FOR QUANTITY AND LOCATIONS.
10 PENETRACIONES DE VENTEO DE TUBERÍAS - VER PLANOS POL PARA CANTIDAD Y POSICIONES.
- 11 CONTINUOUS GUARDRAIL AROUND ROOF WITH ACCESS LADDER - SEE STRUCT DRAWINGS.
11 BARANDILLA CONTINUA ALREDEDOR DE LA CUBIERTA CON ESCALERA DE ACCESO - VER PLANOS DE ESTRUCTURA.
- 12 ROOF GUTTER.
12 CANALÓN DE CUBIERTA.
- 13 RETAINING WALL.
13 MURO DE CONTENCIÓN.
- 14 DOWNSPOUT WITH SPLASHBLOCK.
14 BAJANTE CON SALPICADERO.
- 15 LADDER FOR ROOF ACCESS.
15 ESCALERA DE ACCESO A CUBIERTA.

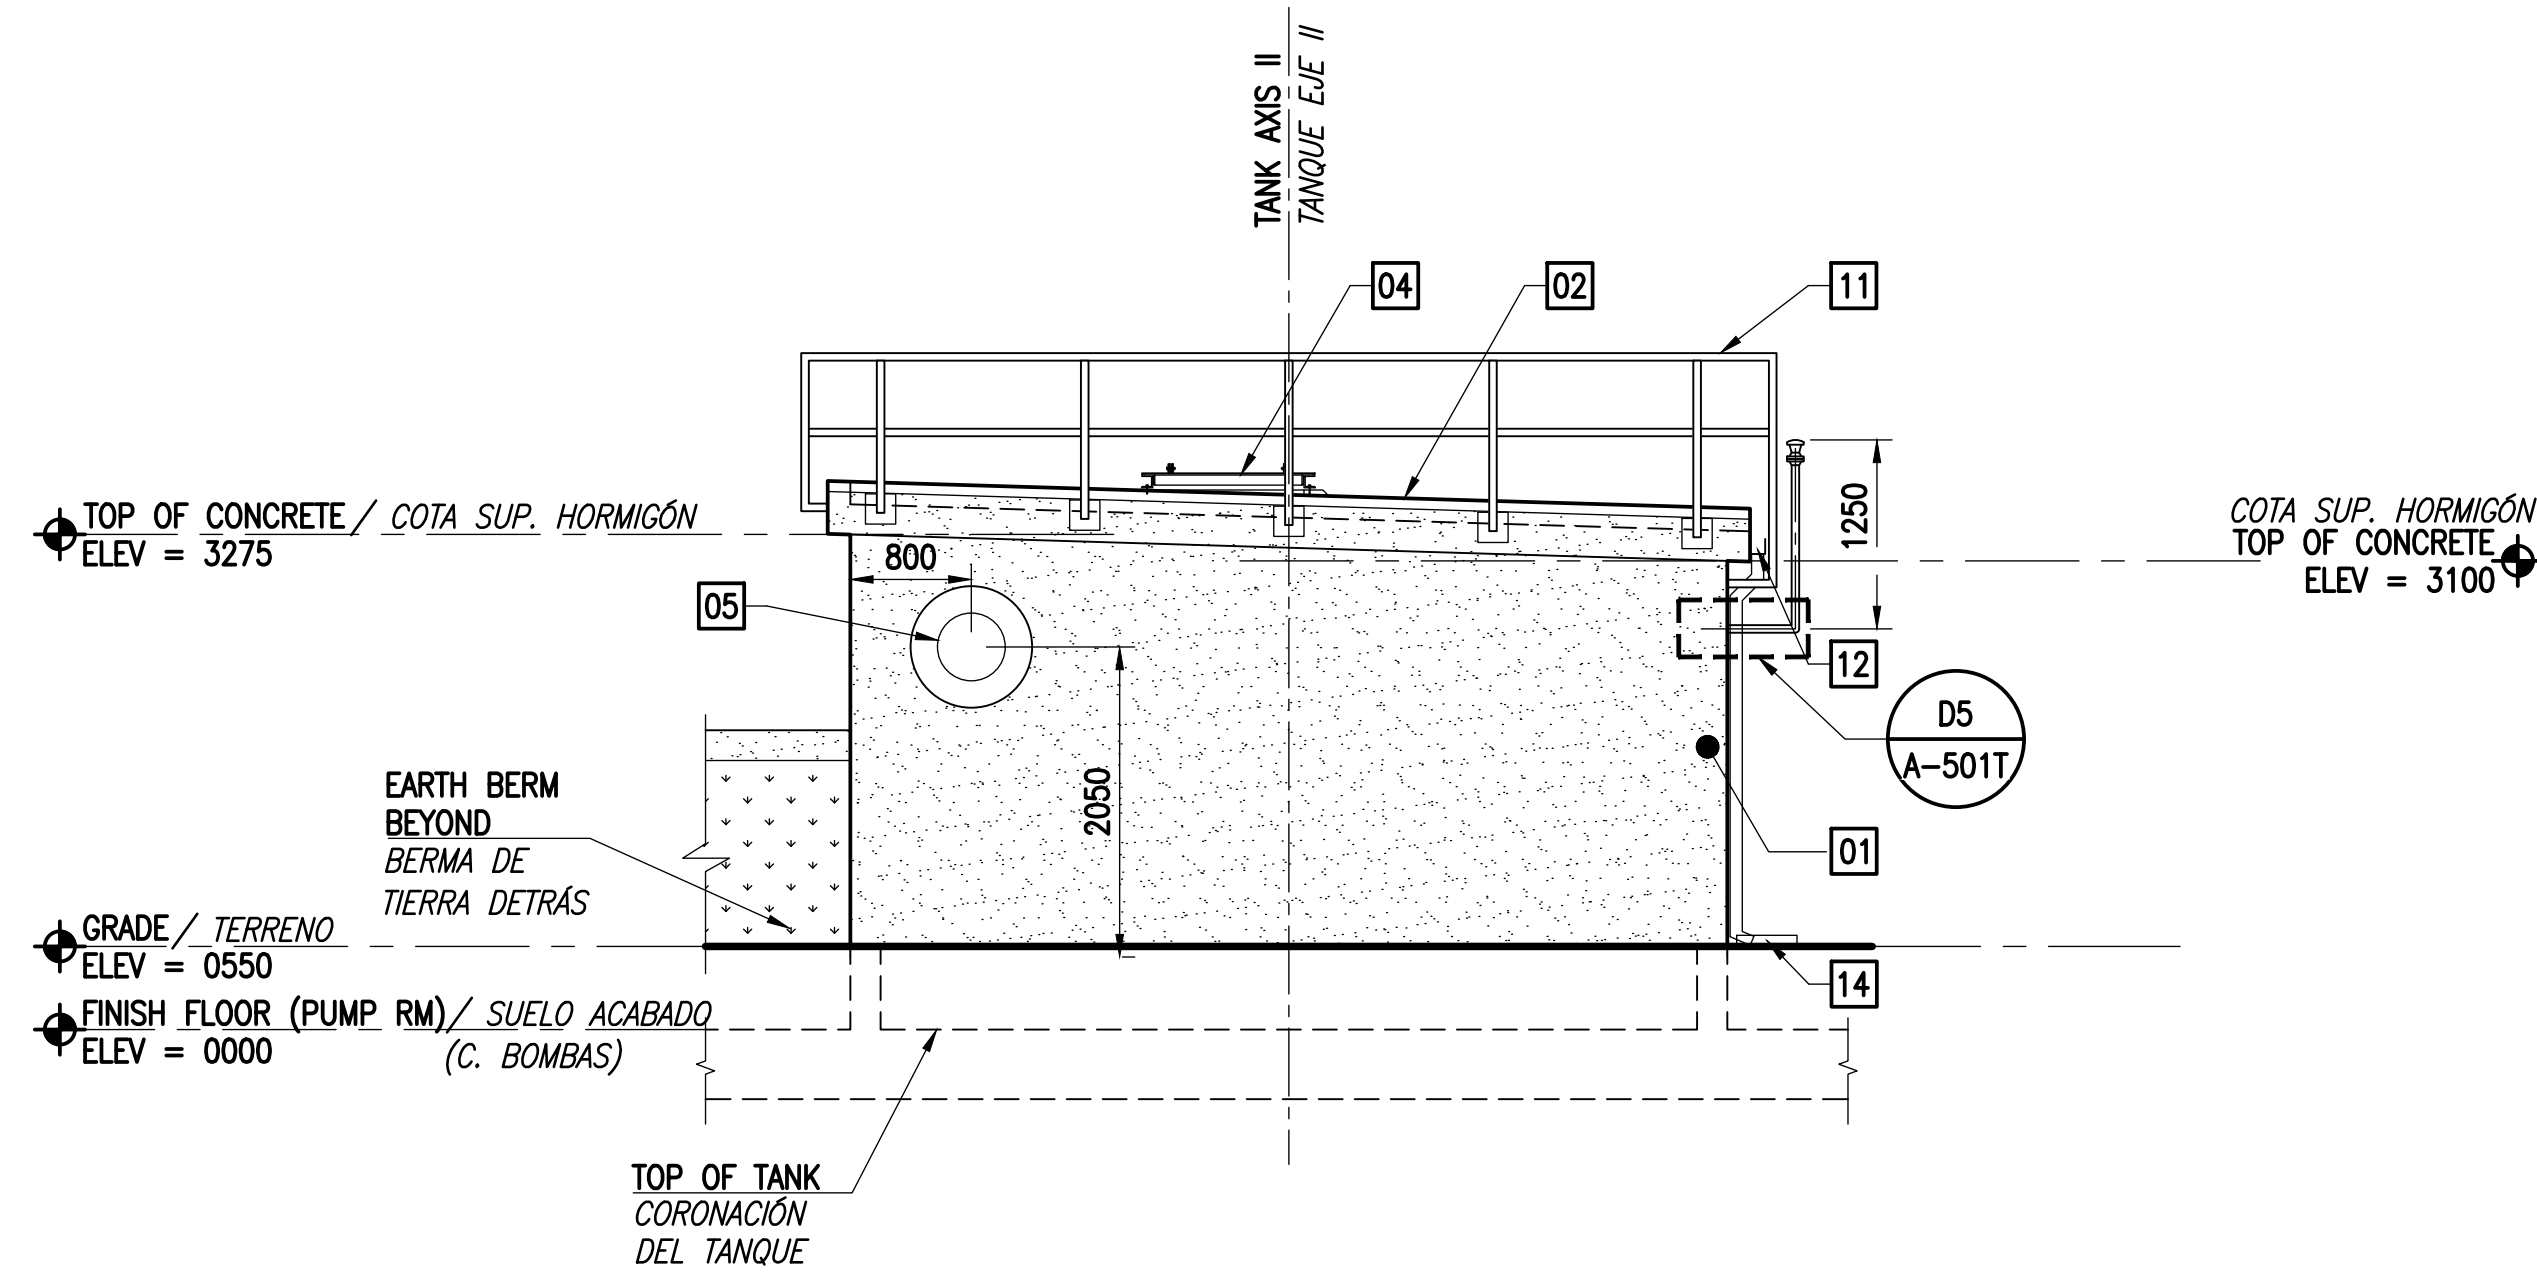

C4 ELEVATION PUMP VAULT / ALZADO CÁMARA DE BOMBAS
SCALE: 1:50

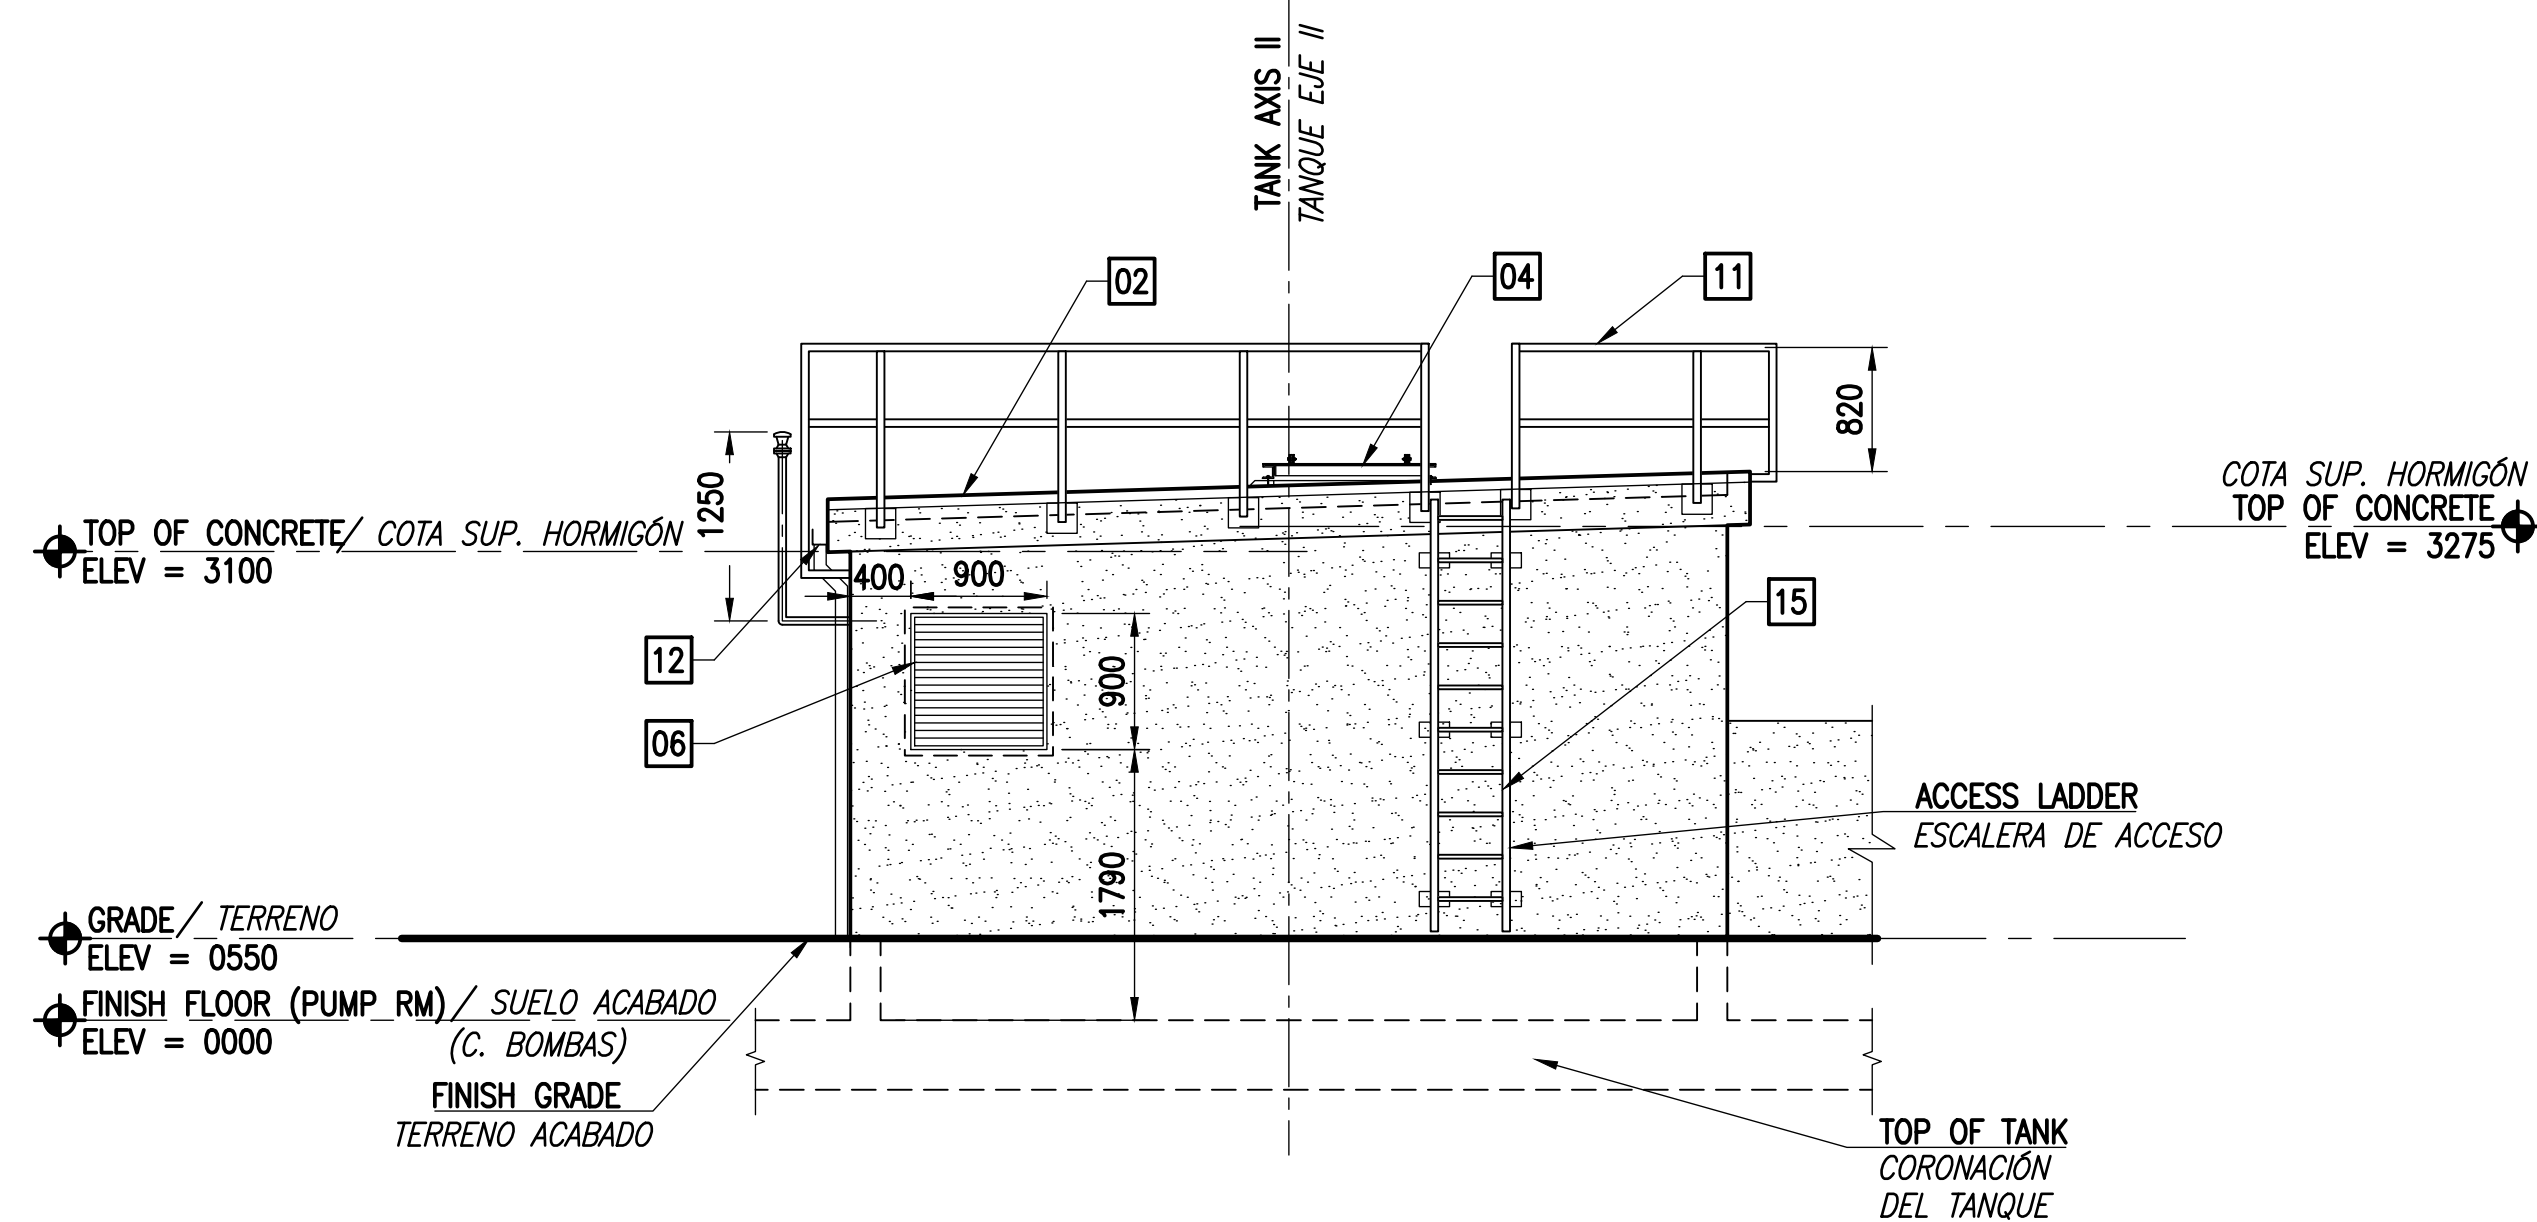


B4 ELEVATION PUMP VAULT / ALZADO CÁMARA DE BOMBAS
SCALE: 1:50

GENERAL NOTES / NOTAS GENERALES

1. DIMENSIONS INDICATED ON ELEVATIONS ARE TO FACE OF CONCRETE OR CENTERLINE OF GUARDRAILS UNLESS OTHERWISE NOTED.
1. LAS DIMENSIONES INDICADAS EN LOS ALZADOS SON A CARA DEL HORMIGÓN O EJE DE BARANDILLAS A MENOS QUE SE INDIQUE OTRA COSA.
2. FLOOR ELEVATIONS ARE RELATIVE. BASE ELEVATION IS AT 32.57.
2. LAS ELEVACIONES DEL SUELO SON RELATIVAS, LA ELEVACIÓN BASE ESTÁ A 32.25.
3. BUILDING ELEVATIONS ARE FOR PUMP VAULT 200. ELEVATIONS FOR PUMP VAULT 100 ARE MIRRORED VERSIONS OF PUMP VAULT 200.
3. LAS ELEVACIONES DEL EDIFICIO SON PARA LA CÁMARA DE BOMBA 200. LAS ELEVACIONES PARA LA CÁMARA DE BOMBAS 100 SON SIMÉTRICAS A LAS DE LA CÁMARA DE BOMBAS 200.

GRAPHIC SCALE(S):
ESCALA(S) GRÁFICA(S):

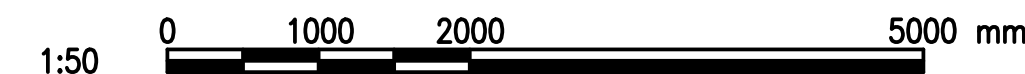

APPROVED	DATE
SYN	DESCRIPTION
COMMONWEALTH OF VIRGINIA SE JIN KWAK Lic. No. 014889 ARCHITECT	
Brockenbrough ENGINEERING & CONSULTING 1011 Boulevard 22020 www.brockenbrough.com	
Stanley Consultants Inc. 225 Iowa Avenue, Muscatine, Iowa 52761-3764 www.stanleyconsultants.com	
APPROVED	A/E INFO
FOR COMMANDER NAVFAC	
ACTIVITY	
SATISFACTORY TO: DATE	
DES	CHK
FM/CM	CCA/EA
BRANCH MANAGER	
DESIGN MANAGER	
FIRE PROTECTION	
XXX	
NAVAL FACILITIES ENGINEERING SYSTEM COMMAND	
NAVAL FACILITIES ENGINEERING SYSTEM COMMAND ~ ATLANTIC	
NORFOLK, VA	
ROTA, SPAIN	
P-919 BULK TANK FARM IMPROVEMENTS, PHASE 1	
BUILDING ELEVATIONS - PUMP VAULTS	
ALZADOS DEL EDIFICIO - CÁMARA DE BOMBAS	
SCALE:	
EPROJECT NO.:	
CONSTR. CONTR. NO.:	
NAVFAC DRAWING NO.:	
14140162	
SHEET	
58 OF 342	
A-403T	



GENERAL NOTES
NOTAS GENERALES

1. BUILDING GRIDS ARE TO CENTERLINE OF CONCRETE WALLS, UNLESS OTHERWISE NOTED.
1. LOS EJES DEL EDIFICIO ESTÁN CENTRADOS CON LOS EJES DE LOS MUROS DE HORMIGÓN, A MENOS QUE SE INDIQUE OTRA COSA.
2. DIMENSIONS INDICATED ON PLANS ARE TO CENTERLINE OF WALLS, FACE OF FINISHES, OR FACE OF PURLINS, UNLESS OTHERWISE NOTED.
2. LAS DIMENSIONES INDICADAS EN LAS PLANTAS ESTÁN A EJE DE MUROS, CARA DE ACABADOS, O CARA DE CORREAS, A MENOS QUE SE INDIQUE OTRA COSA.
3. FLOOR ELEVATIONS ARE RELATIVE. BASE ELEVATION IS AT 29.20.
3. LAS ELEVACIONES DE SUELO SON RELATIVAS. LA ELEVACIÓN BASE ES 29.20.
4. SEE MECHANICAL, ELECTRICAL AND PLUMBING DRAWINGS FOR ADDITIONAL INFORMATION.
4. VER LOS PLANOS DE MECÁNICA, ELECTRICIDAD Y FONTANERÍA PARA INFORMACIÓN ADICIONAL.

Age Group	Number of People
15-19	1000
20-24	1500
25-29	2000
30-34	2500
35-39	3000
40-44	3500
45-49	4000
50-54	4500
55-59	5000
60-64	4800
65-69	4600
70-74	4400
75-79	4200
80-84	4000
85-89	3800
90-94	3600
95-99	3400


21-05 A



SCALE: 1 : 50
ESCALA: 1 : 50

GENERAL NOTES
NOTAS GENERALES


1. LOCATION OF MECHANICAL AND ELECTRICAL ITEMS ARE SHOWN FOR COORDINATION AND GENERAL LOCATION ONLY. REFERENCE MECHANICAL AND ELECTRICAL DRAWINGS FOR QUANTITIES AND SPECIFIC INFORMATION FOR THESE ITEMS.
1. LA POSICIÓN DE LOS ELEMENTOS MECÁNICOS Y ELÉCTRICOS SE MUESTRAN SÓLO PARA COORDINACIÓN Y UBICACIÓN GENERAL. REFERIRSE A LOS PLANOS DE MECÁNICA Y DE ELECTRICIDAD PARA CANTIDADES E INFORMACIÓN ESPECÍFICA DE ESTOS ELEMENTOS.
2. SHEET A-001 FOR CEILING SYMBOLS.
2. VER PLANO A-001 PARA SÍMBOLOS DE TECHO.

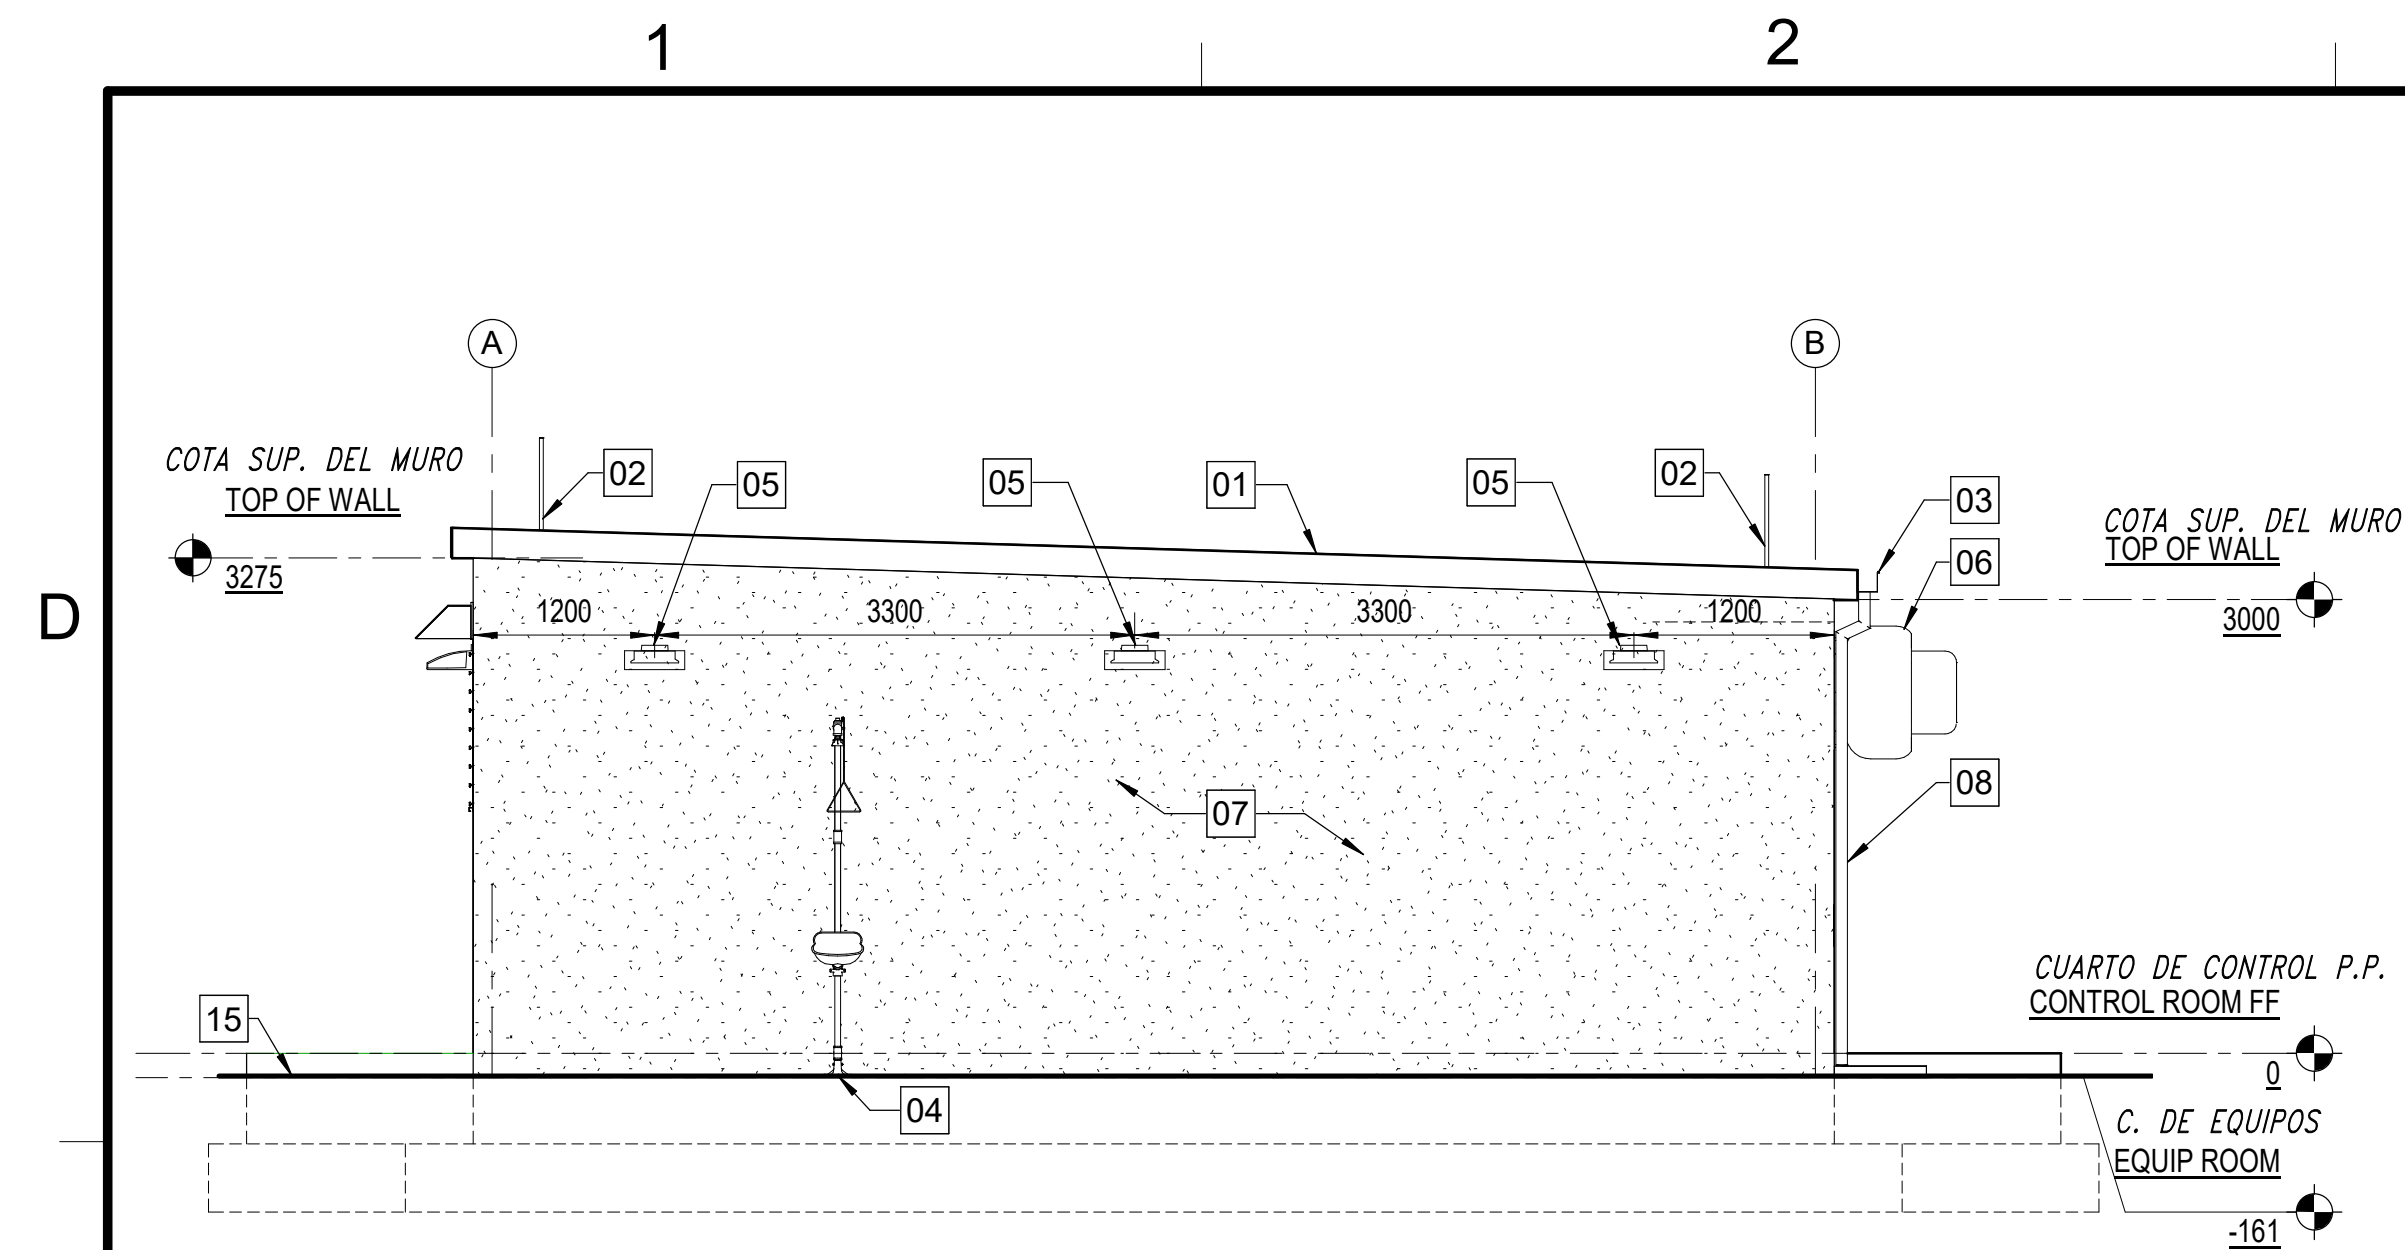


WEST ELEVATION
ALZADO OESTE

C1


SCALE: 1 : 50
ESCALA: 1 : 50

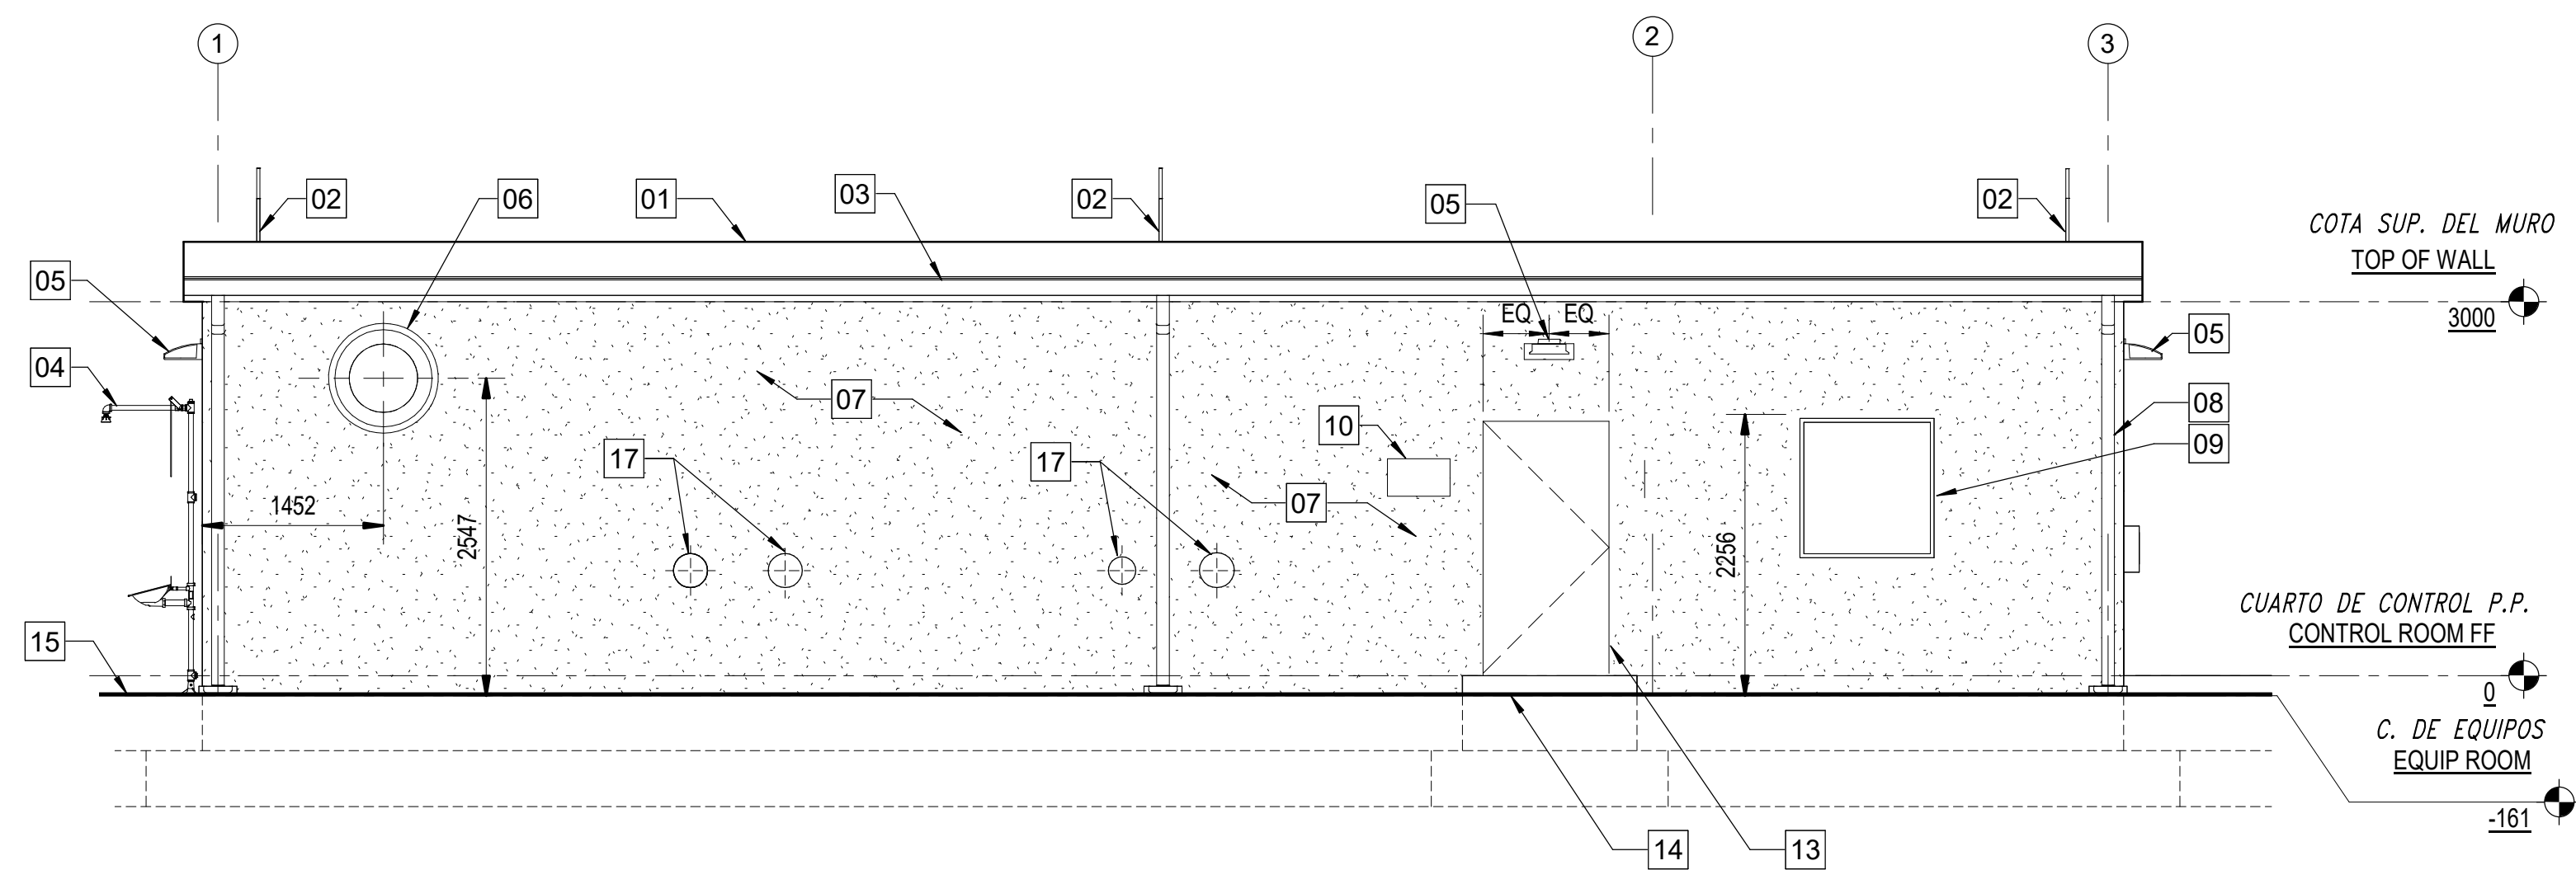

SOUTH ELEVATION
ALZADO SUR
SCALE: 1 : 50
ESCALA: 1 : 50

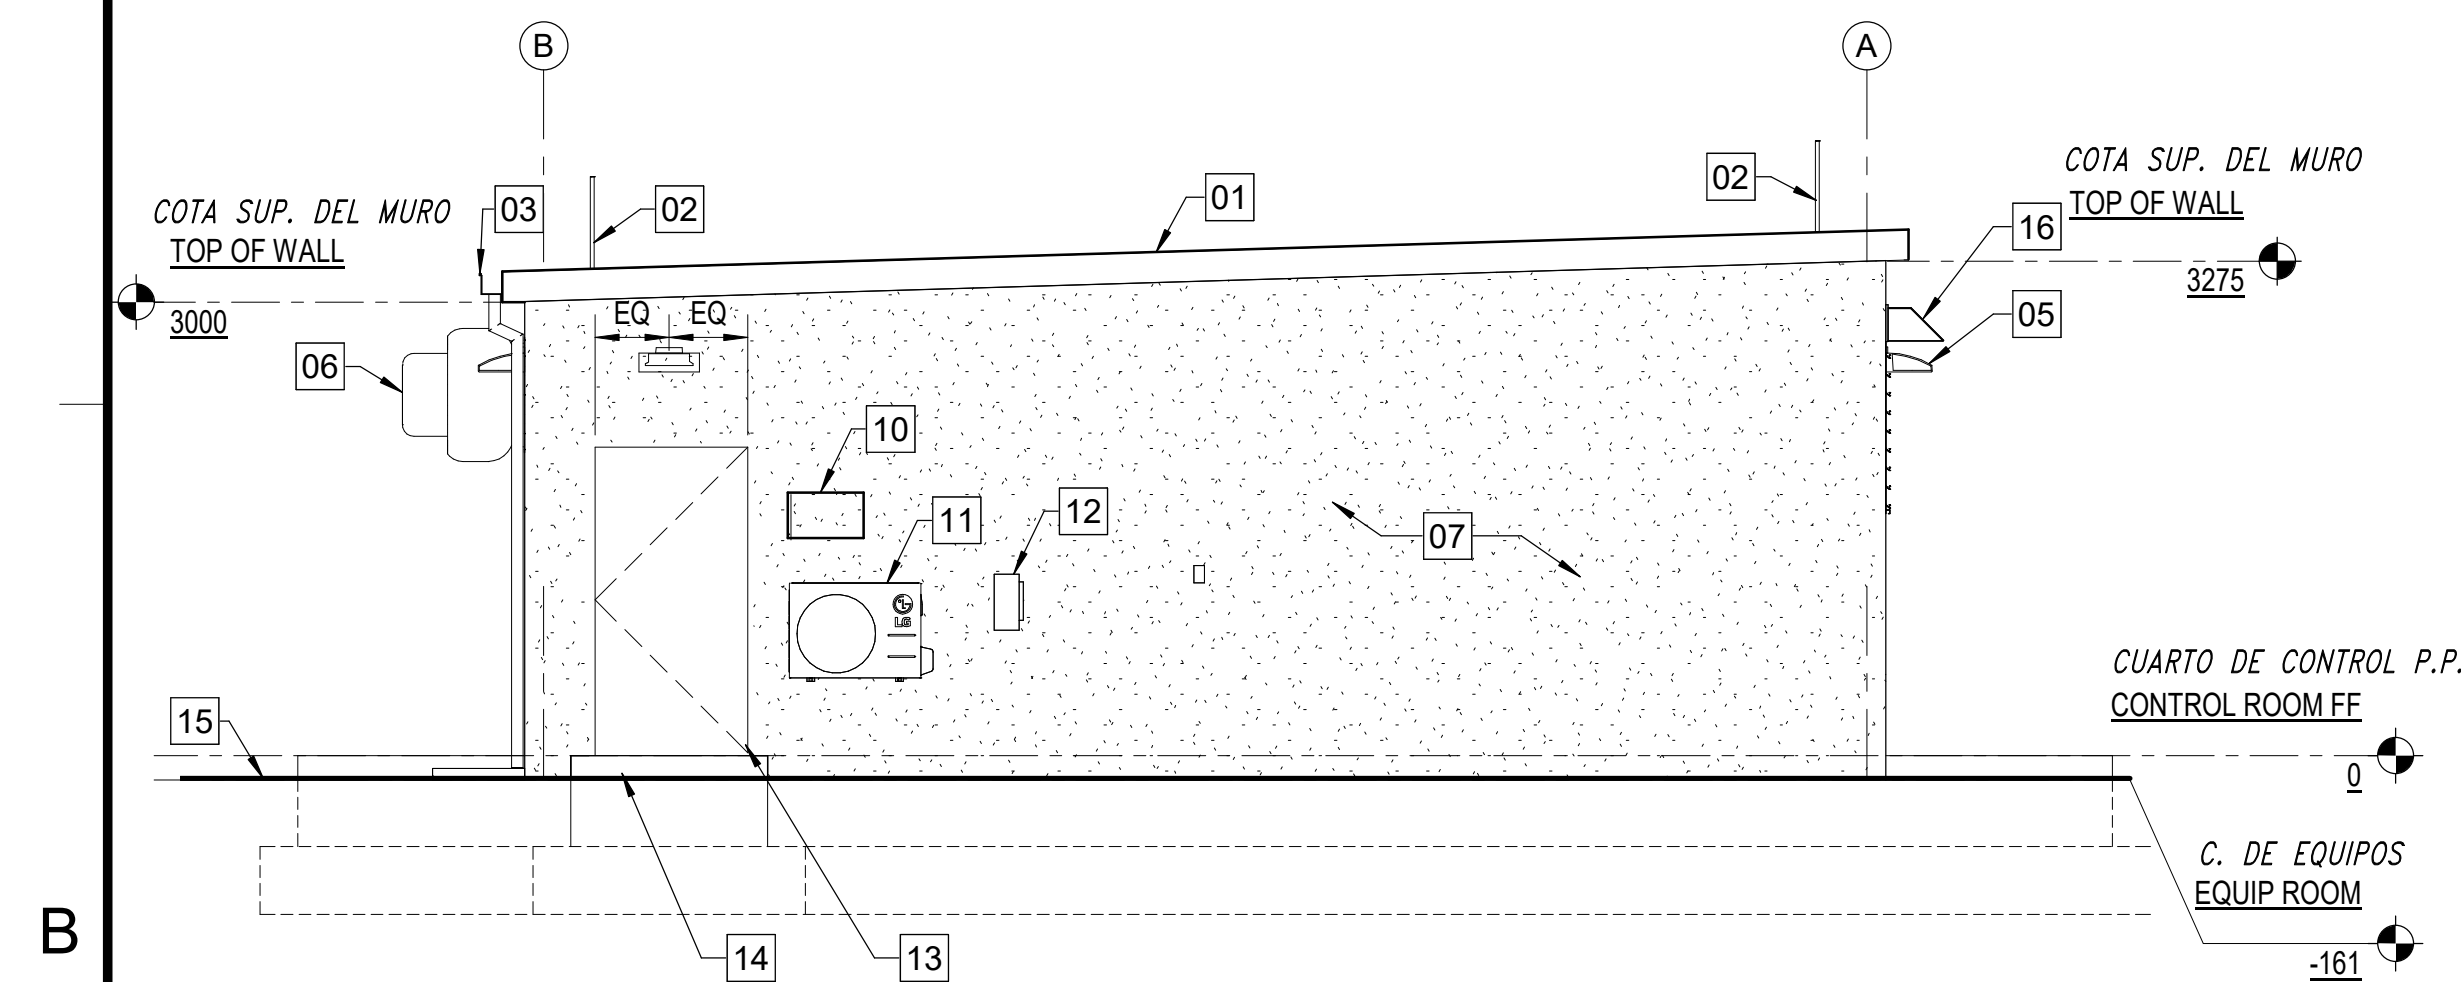

B1 EAST ELEVATION
ALZADO ESTE
SCALE: 1:50
ESCALA: 1:50

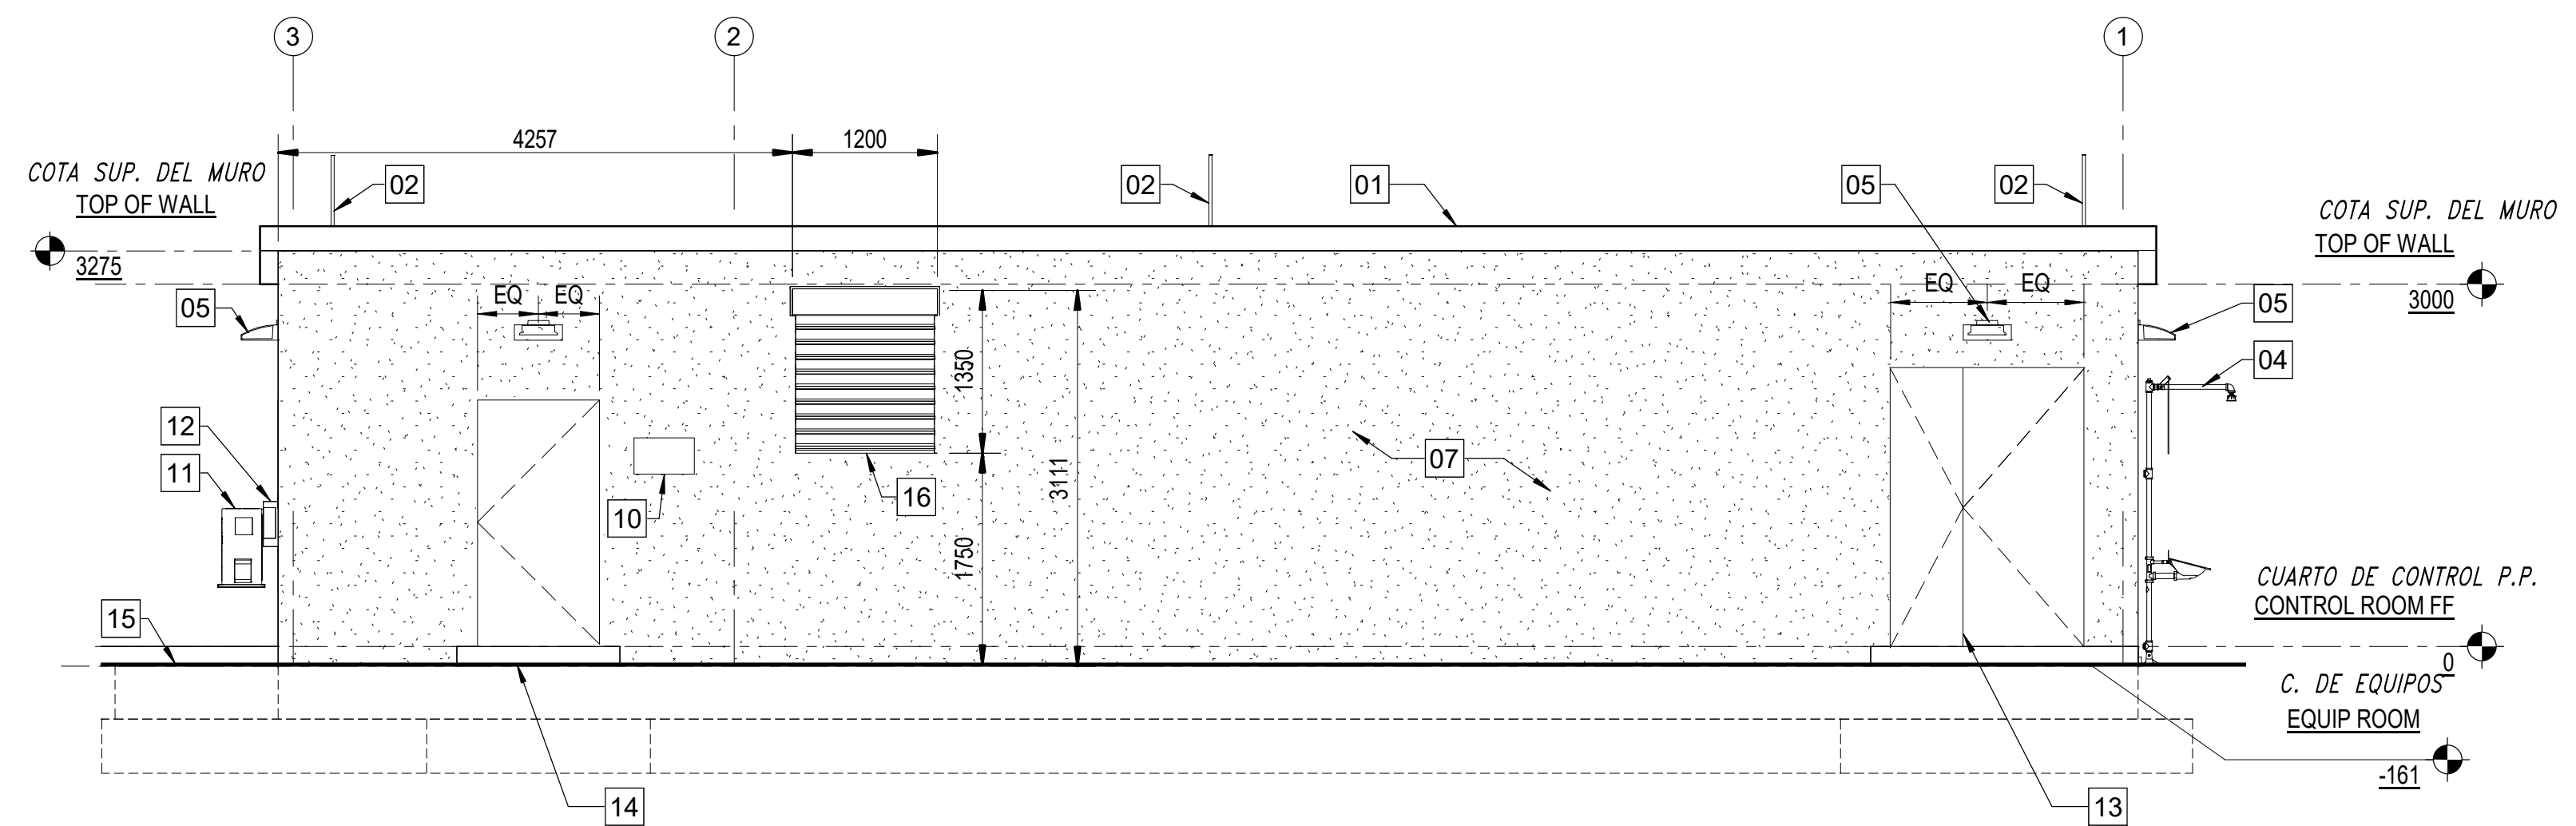

NORTH ELEVATION
ALZADO NORTE
SCALE: 1:50
ESCALA: 1:50

KEYED NOTES #


NOTAS DE REFERENCIA

- | | | | |
|----|--|-----|--|
| 01 | FLUID-APPLIED ELASTOMERIC ROOFING, 3% SLOPE. | 10 | BUILDING SIGN PER BASE STANDARDS. |
| 01 | CUBIERTA ELASTOMÉRICA DE APLICACIÓN FLUIDA, PENDIENTE 3%. | 10 | SEÑAL DEL EDIFICIO SEGÚN NORMAS DE LA BASE. |
| 02 | LIGHTNING PROTECTION AIR TERMINAL - SEE ELECT, TYP. | 11 | DUCTLESS AIR CONDITIONER UNIT - SEE MECHANICAL DRAWINGS. |
| 02 | TERMINAL DE PARARRAYOS - VER ELECTRICIDAD, TIP. | 11 | EQUIPO DE AIRE ACONDICIONADO SIN CONDUCTOS - VER PLANOS DE MECÁNICA. |
| 03 | ROOF GUTTER. | 12 | WEATHER PROOF FUSED DISCONNECT MOUNT ADJACENT TO UNIT. |
| 03 | CANALÓN DE CUBIERTA. | 12 | DESCONECTADOR RESISTENTE A INTEMPERIE MONTADO JUNTO AL EQUIPO. |
| 04 | EMERGENCY EYEWASH AND SHOWER - SEE PLUMBING DRAWINGS. | 13 | STEEL PLATE SPLINTER DOORS, TYPICAL. |
| 04 | LAVAJOS Y DUCHA DE EMERGENCIA - VER PLANOS DE FONTANERÍA. | 13 | PUERTAS ABATIBLES CON CHAPA METÁLICA, TÍPICO. |
| 05 | WALL MOUNTED EXTERIOR LIGHT FIXT CENTERED OVER DOORS - SEE ELECTRICAL DWGS (TYP). | 14 | CONCRETE LANDING - SEE CIVIL DRAWINGS. |
| 05 | LUMINARIA EXTERIOR MONTADA EN PARED CENTRADA SOBRE LAS PUERTAS - VER ELECTRICIDAD. | 14 | RELLANO DE HORMIGÓN - VER PLANOS DE URBANIZACIÓN. |
| 06 | EXHAUST FAN - SEE MECHANICAL DRAWINGS. | 15. | FINISH GRADE. |
| 06 | EXTRACTOR - VER PLANOS DE MECÁNICA. | 15 | TERRENO ACABADO. |
| 07 | CONCRETE WALL, STUCCO, PAINTED. | 16 | WEATHERPROOF COMBINATION LOUVER/DAMPER WITH SECURITY GRILLE- SEE MECHANICAL DRAWINGS. |
| 07 | MURO DE HORMIGÓN, ENFOSCADO, PINTADO. | 16 | COMBINACIÓN REJILLA/COMPUERTA PARA INTEMPERIE CON REJILLA DE SEGURIDAD - VER PLANOS DE MECÁNICA. |
| 08 | DOWNSPOUT & SPLASHBLOCK. | 17. | PIPE PENETRATIONS, TYPICAL. - SEE MECHANICAL DRAWINGS FOR LOCATION AND SIZE. SEE A1/A-511 FOR DETAIL. |
| 08 | BAJANTE CON SALPICADERO. | 17 | PENETRACIONES DE TUBERÍAS, TÍPICO. - VER PLANOS DE MECÁNICA PARA UBICACIÓN Y TAMAÑO. VER A1/A-511 PARA DETALLES. |
| 09 | STEEL WINDOW, 1140 x 1180 mm. | | |
| 09 | VENTANA DE ACERO, 1140 x 1180 mm. | | |

GENERAL NOTES
NOTAS GENERALES

1. DIMENSIONS INDICATED ON ELEVATIONS ARE TO FACE OF CONCRETE OR CENTERLINE OF EQUIPMENT, UNLESS OTHERWISE NOTED.
1. LAS DIMENSIONES INDICADAS EN LOS ALZADOS SON A CARA DE HORMIGÓN O EJE DE EQUIPO, A MENOS QUE SE INDIQUE OTRA COSA.
2. FLOOR ELEVATIONS ARE RELATIVE. BASE ELEVATION IS AT 29.20.
2. LAS ELEVACIONES DE SUELO SON RELATIVAS. LA ELEVACIÓN BASE ESTÁ A 29.20.
3. SEE MECHANICAL, ELECTRICAL AND PLUMBING DRAWINGS FOR ADDITIONAL INFORMATION.
3. VER PLANOS DE MECÁNICA, ELECTRICIDAD Y FONTANERÍA PARA INFORMACIÓN ADICIONAL.

GRAPHIC SCALE(S):
ESCALA(S) GRÁFICA(S):

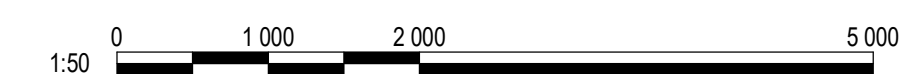[illegible]







FILE NAME: G:\21 Jobs\21-015 FY 23 MILCON P-919 Bulk Tanks - Rota\ADVA-A-501T DETAILS.dwg LAYOUT NAME: A-501 PLOTTED: Tuesday, June 25, 2024 - 8:32am USER: okogma

D


C

B

A

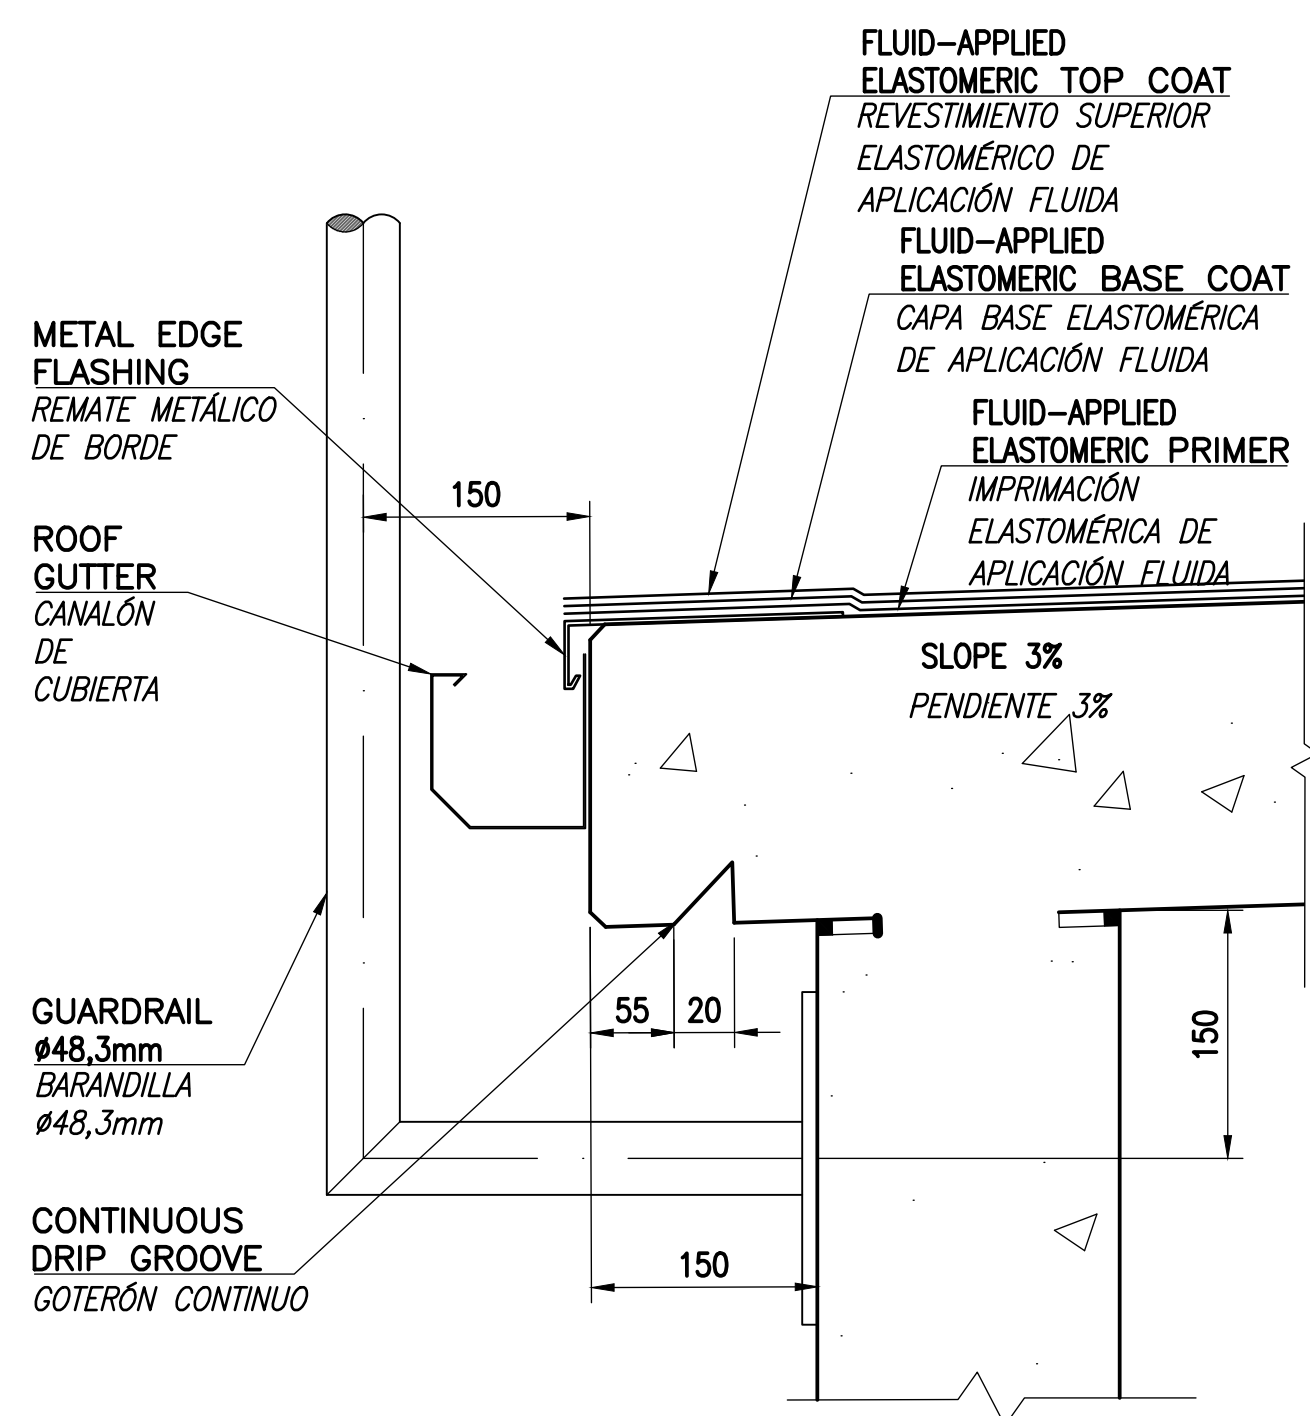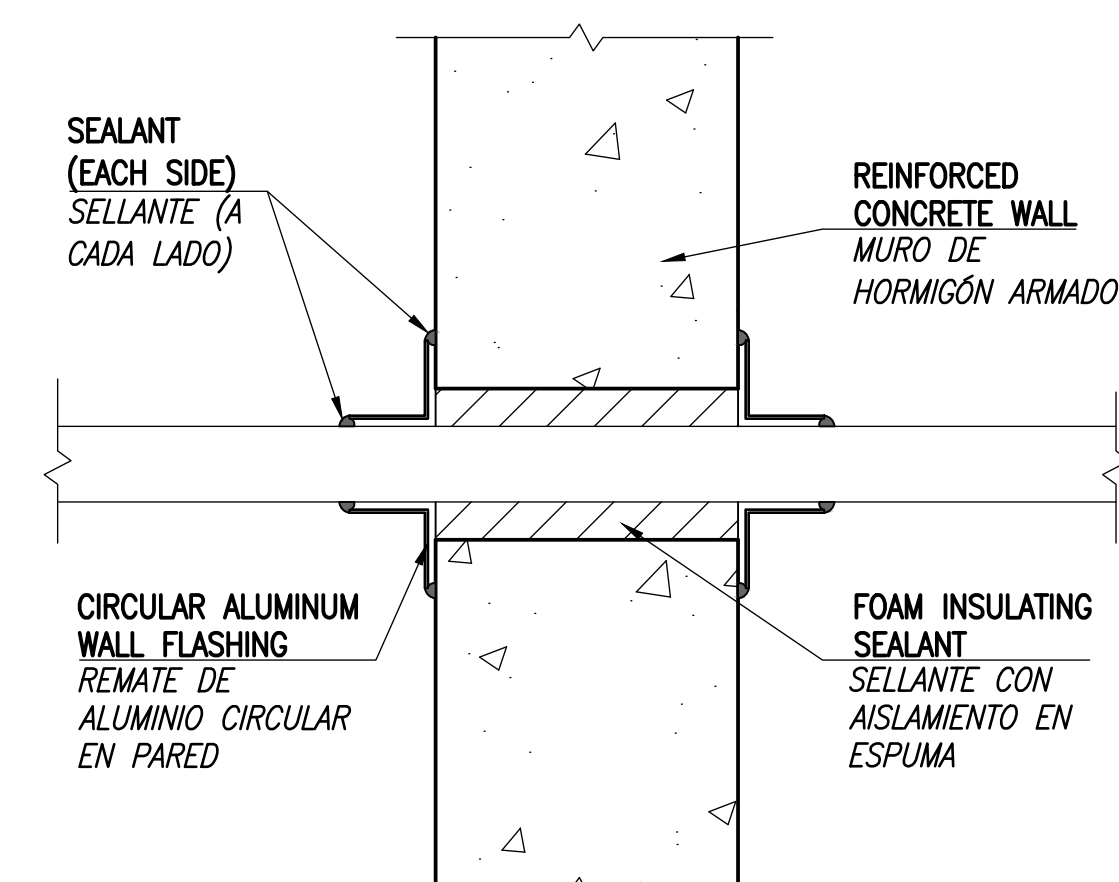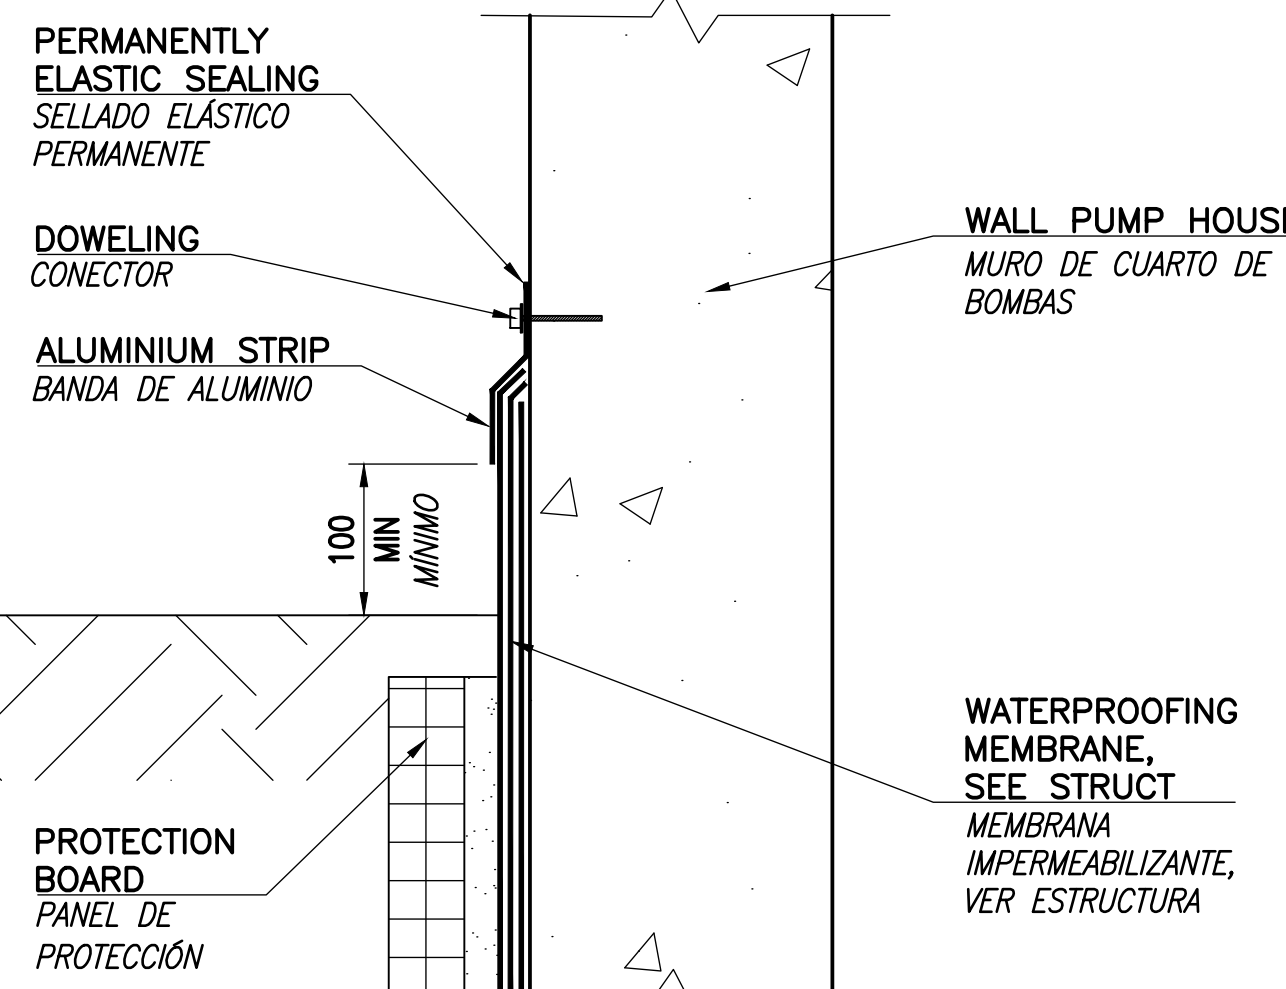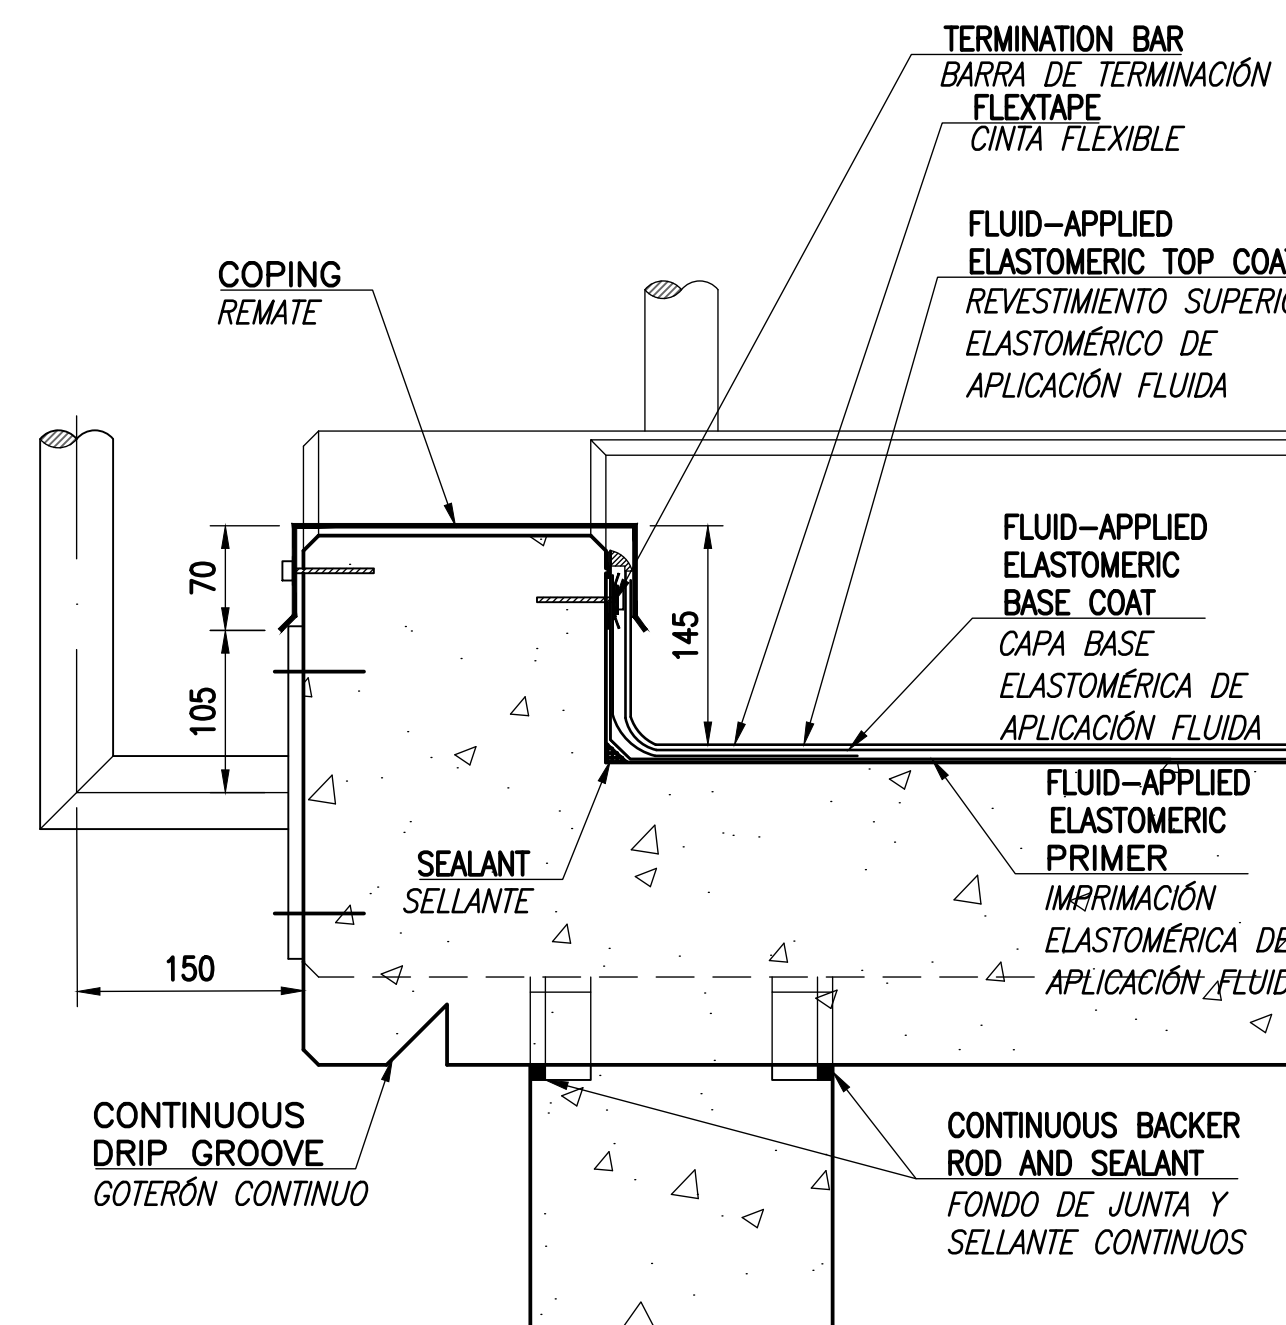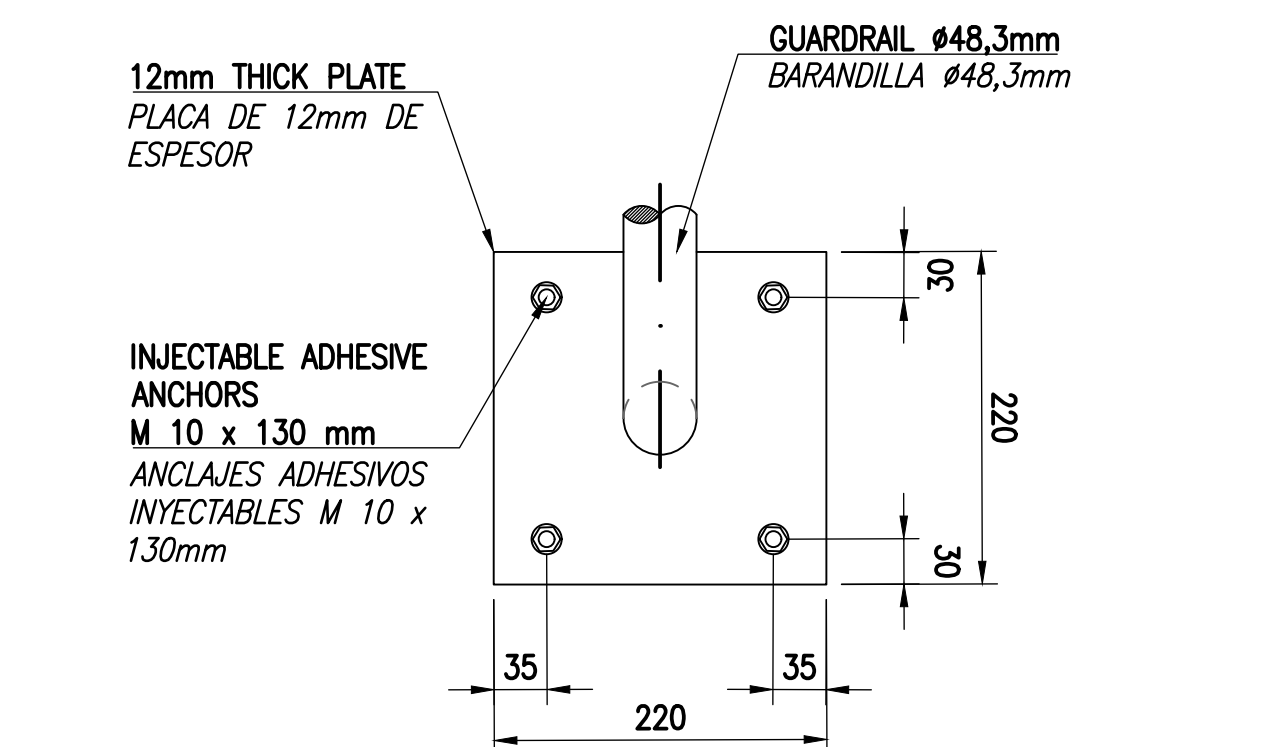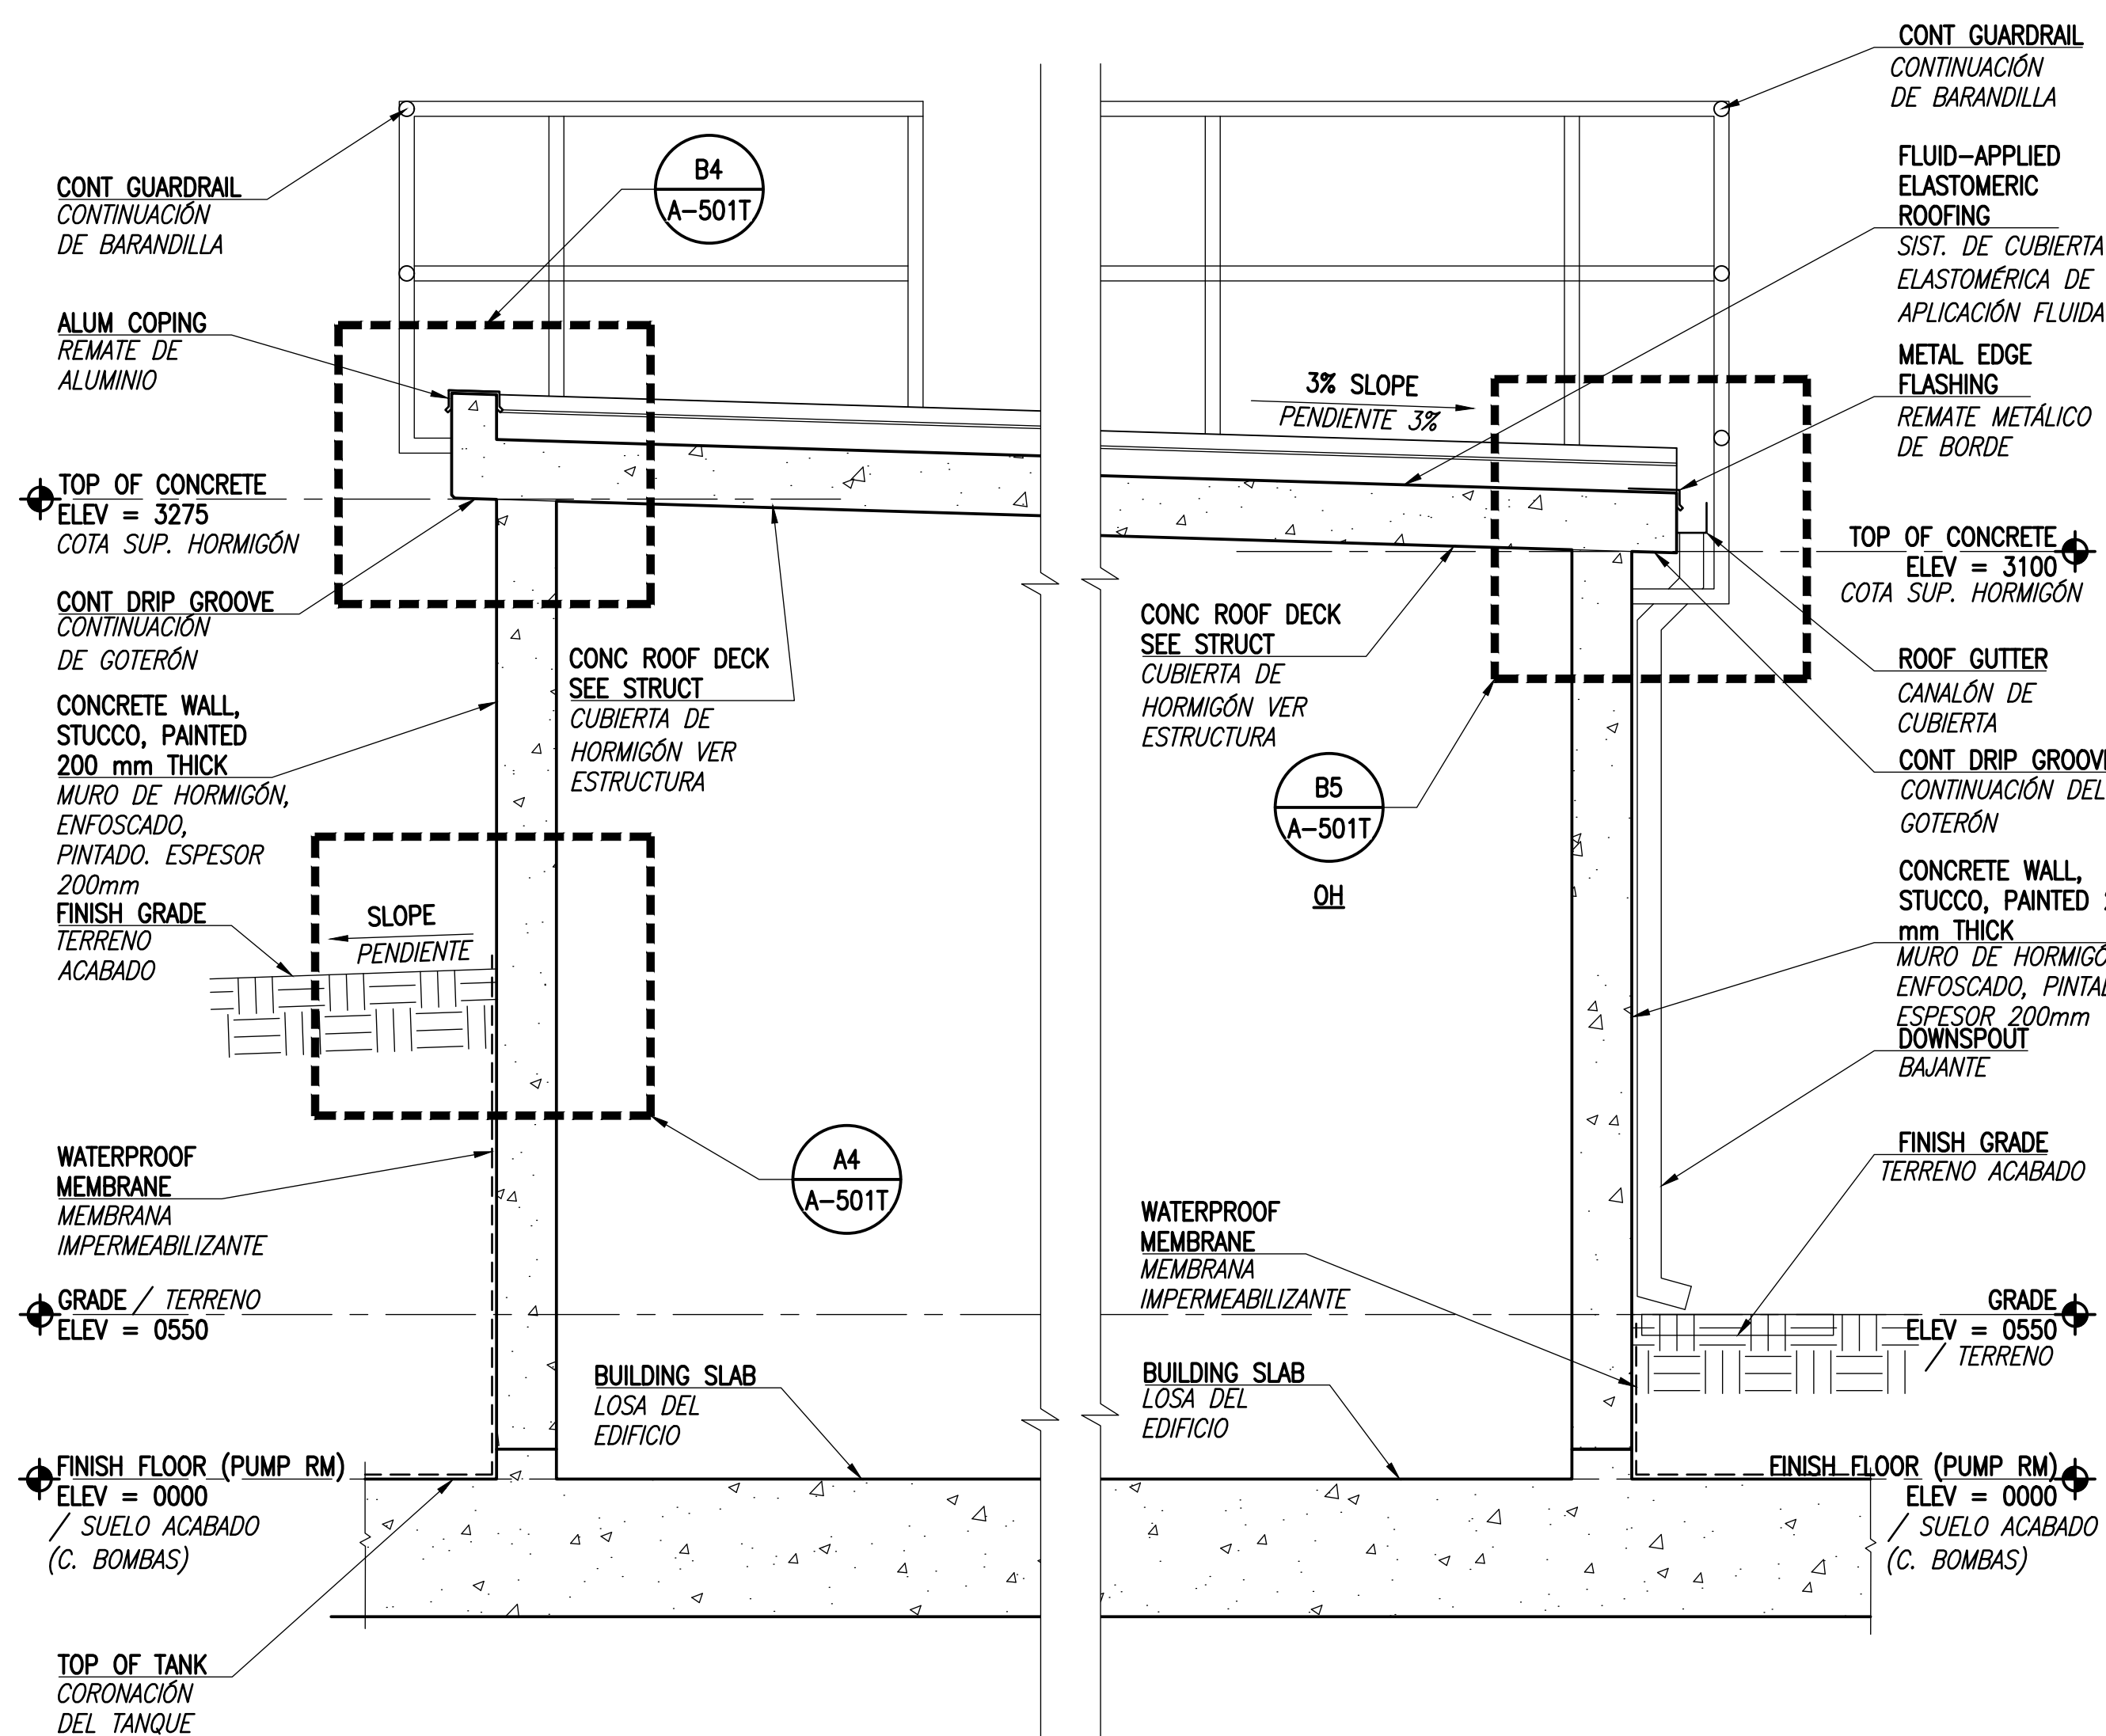



GRAPHIC SCALE(S):
ESCALA(S) GRÁFICA(S):

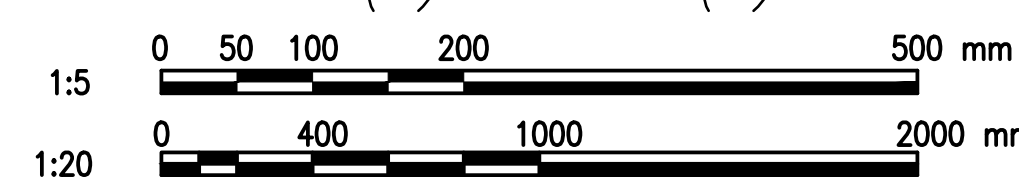


APPROVED	DATE	DESCRIPTION	REV
NAVFAC			
COMMONWEALTH OF VIRGINIA			
SE JIN KWAK Lic. No. 014889 ARCHITECT			
Brockenbrough ENGINEERING & CONSULTING 1001 Boulevard 220 Iowa Avenue, Martinsburg, Iowa 52761-3764 www.brockenbrough.com			
Stanley Consultants Inc. 220 Iowa Avenue, Martinsburg, Iowa 52761-3764 www.stanleyconsultants.com			
APPROVED			
FOR COMMANDER NAVFAC			
ACTIVITY			
SATISFACTORY TO: DATE			
DES	CHK	DRW	CHK
SJK	SJK	SJK	KWH
PM/CM	CC/EA	CC/EA	CC/EA
BRANCH MANAGER			
DESIGN MANAGER			
FIRE PROTECTION			
XXX			
NAVAL FACILITIES ENGINEERING SYSTEM COMMAND			
NAVAL FACILITIES ENGINEERING SYSTEM COMMAND ~ ATLANTIC			
ATLANTIC DESIGN AND CONSTRUCTION			
NAVAL STATION ROTA			
ROTA, SPAIN			
P-919 BULK TANK FARM IMPROVEMENTS, PHASE 1			
DETAILS - PUMP VAULTS			
DETALLES - CÁMARAS DE BOMBAS			
SCALE:			
PROJECT NO.:			
CONSTR. CONTR. NO.:			
NAVFAC DRAWING NO.:			
14140169			
SHEET			
65 OF 342			
A-501T			
NAVFAC METRIC DRAWING REVISION: 07 AUGUST 2018			




SCALE: 1:5
ESCALA: 1 : 5

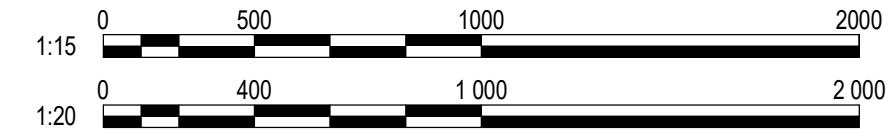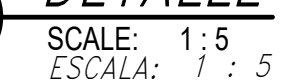


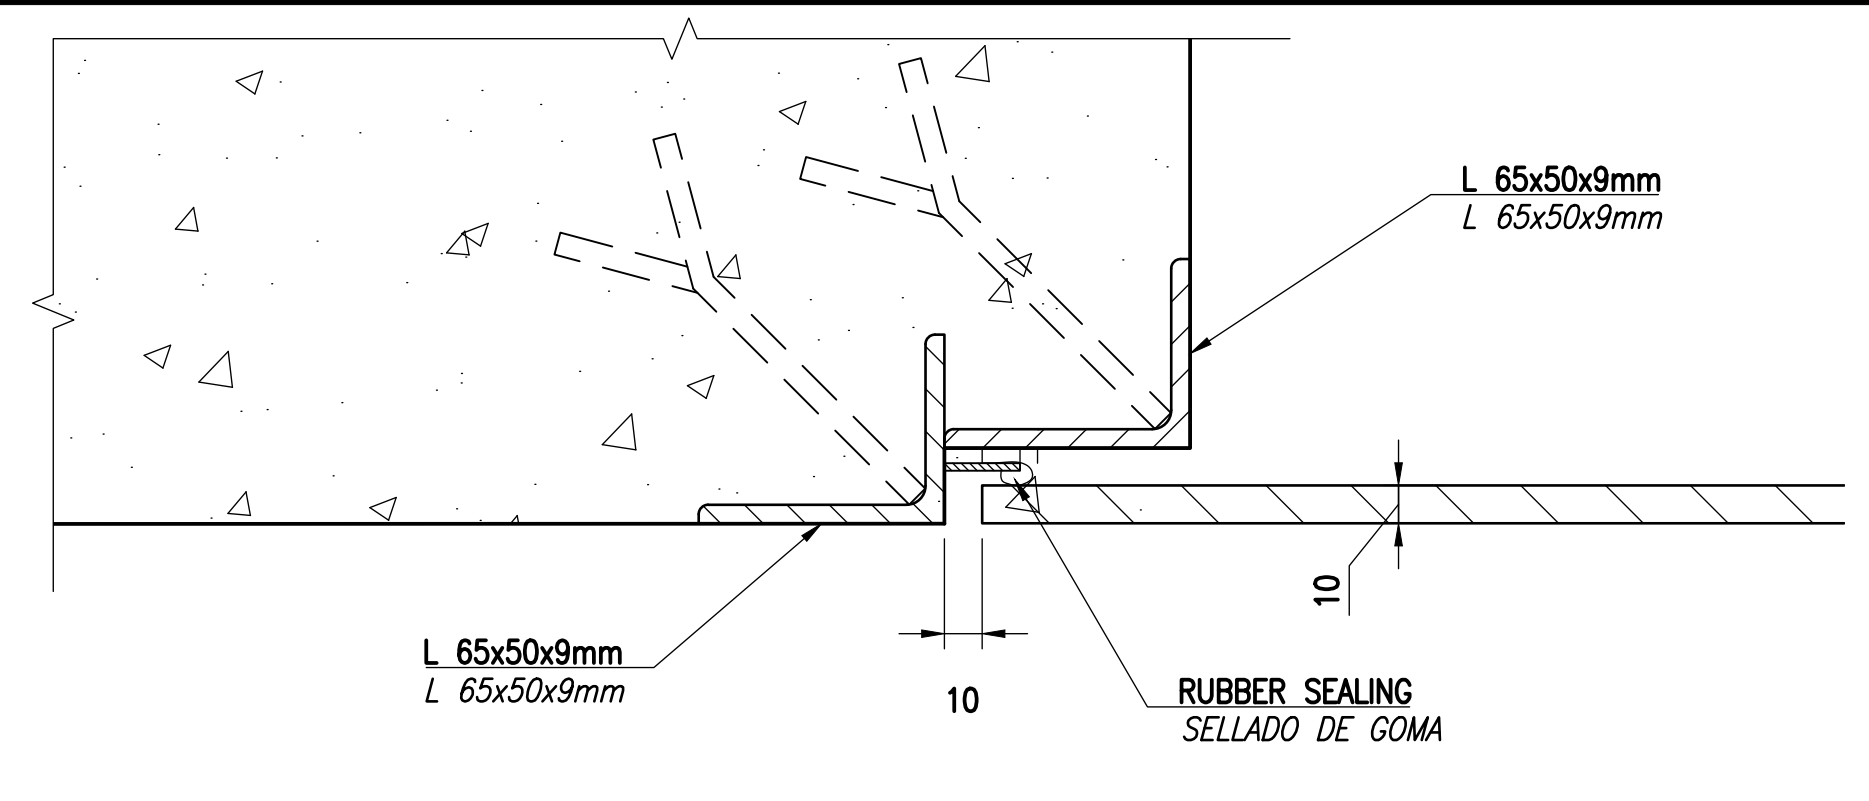


D4 LATCH DETAIL
DETALLE DEL CIERRE
SCALE: 1:2
ESCALA: 1:2

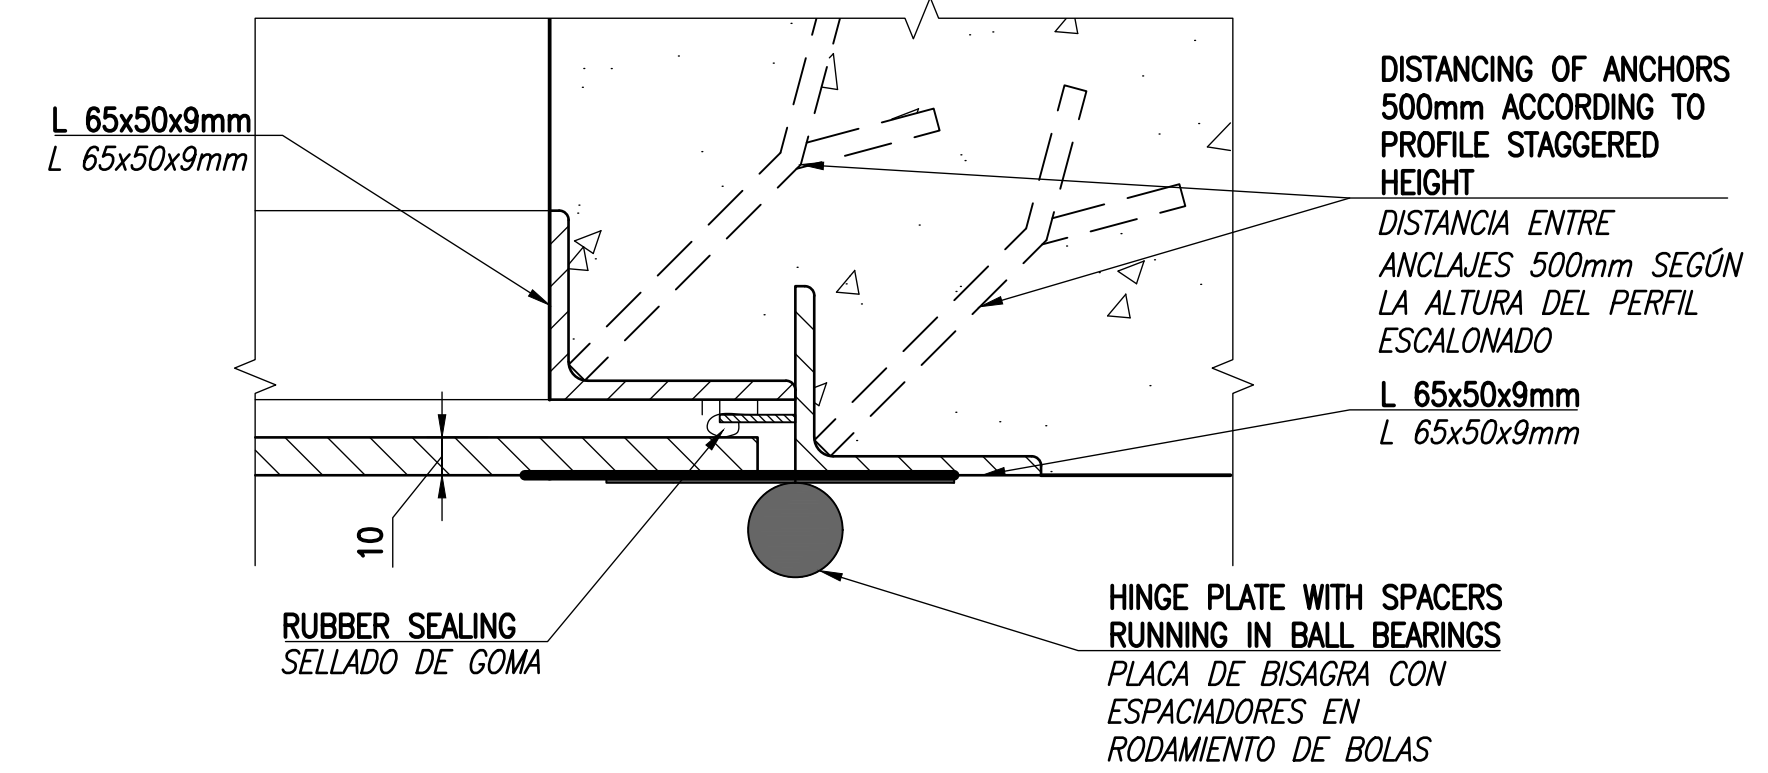

C4 HINGE DETAIL
DETALLE DE BISAGRA
SCALE: 1:2
ESCALA: 1:2

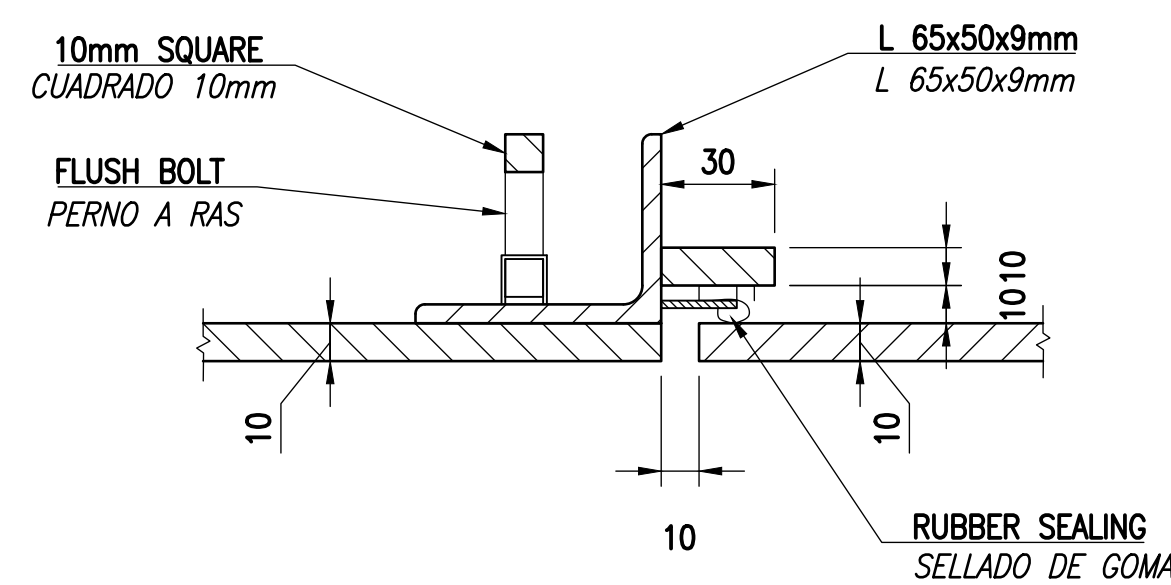


B4 ASTRAGAL DETAIL
DETALLE DE ASTRÁGALO
SCALE: NONE
ESCALA: NINGUNA

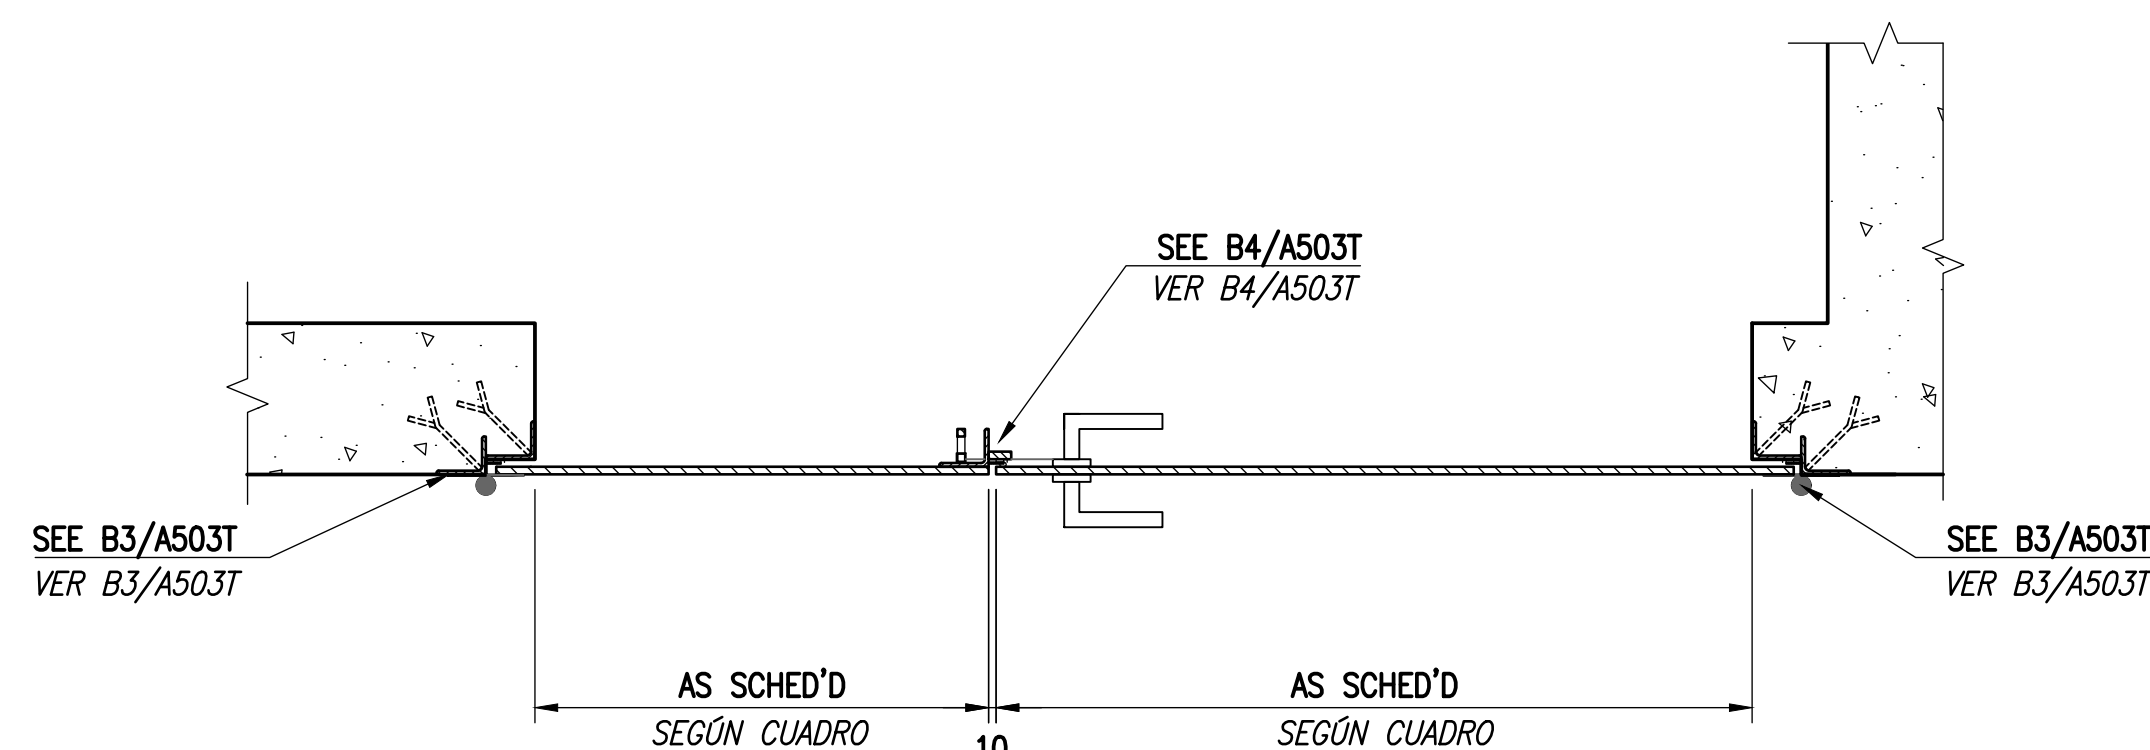

DETAIL
DETALLE

A3

SCALE: 1:10
ESCALA: 1:10

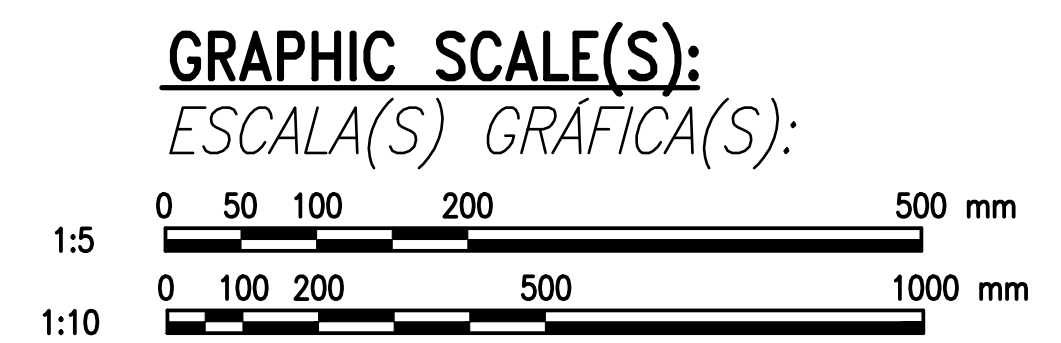


FILE NAME: G:\21 Jobs\21-015 FY 23 MILCON P-919 Bulk Tanks - Rota\CAD\VA-A-504T DETAILS.dwg LAYOUT NAME: A-503T PLOTTED: Tuesday, June 25, 2024 - 8:33am USER: olegina

D


C

B


A

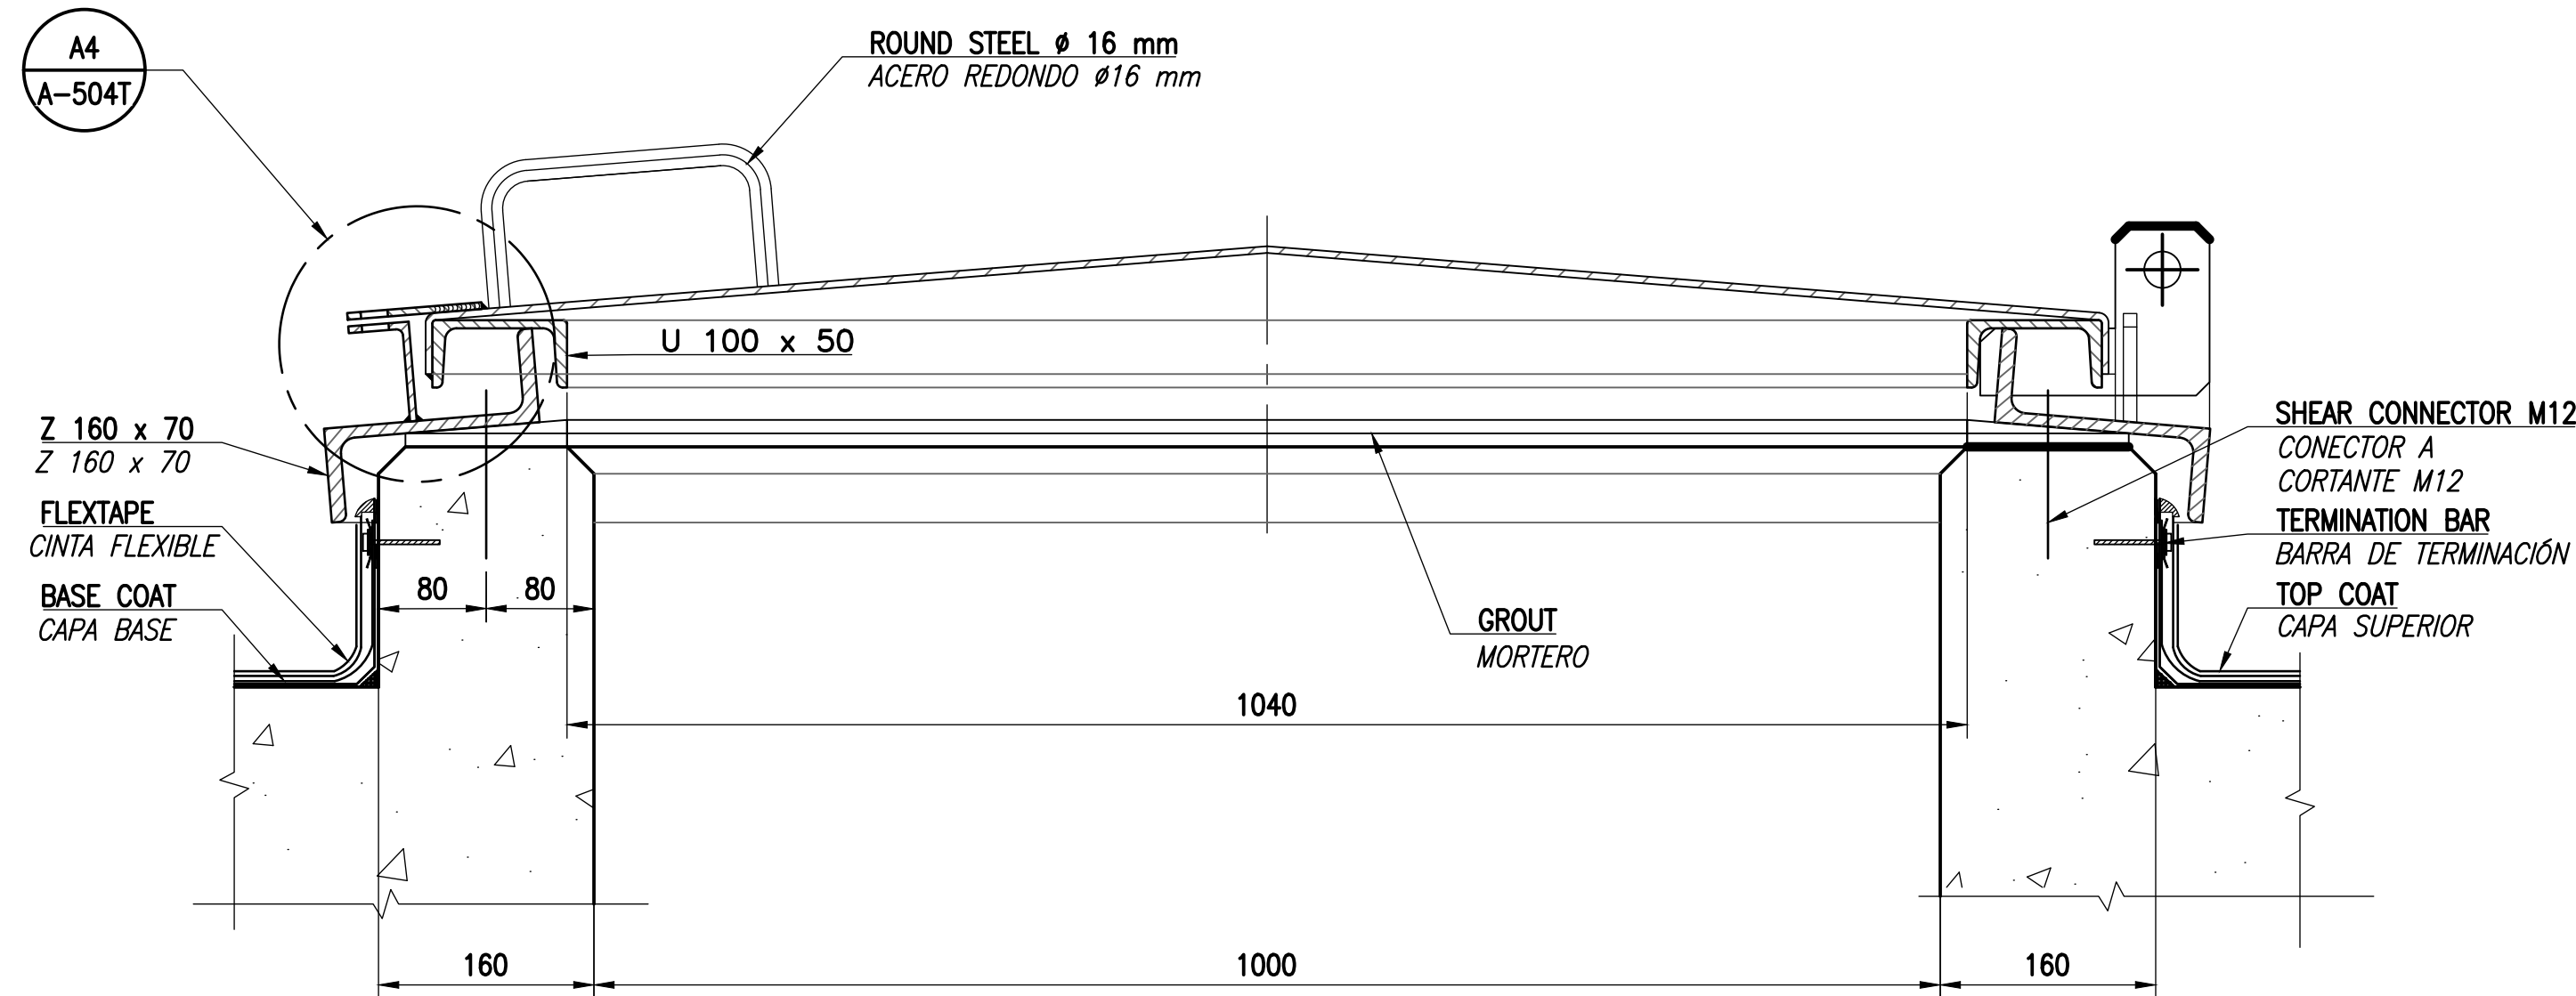


C1
SECTION
SECCIÓN
SCALE: 1:5
ESCALA: 1:5

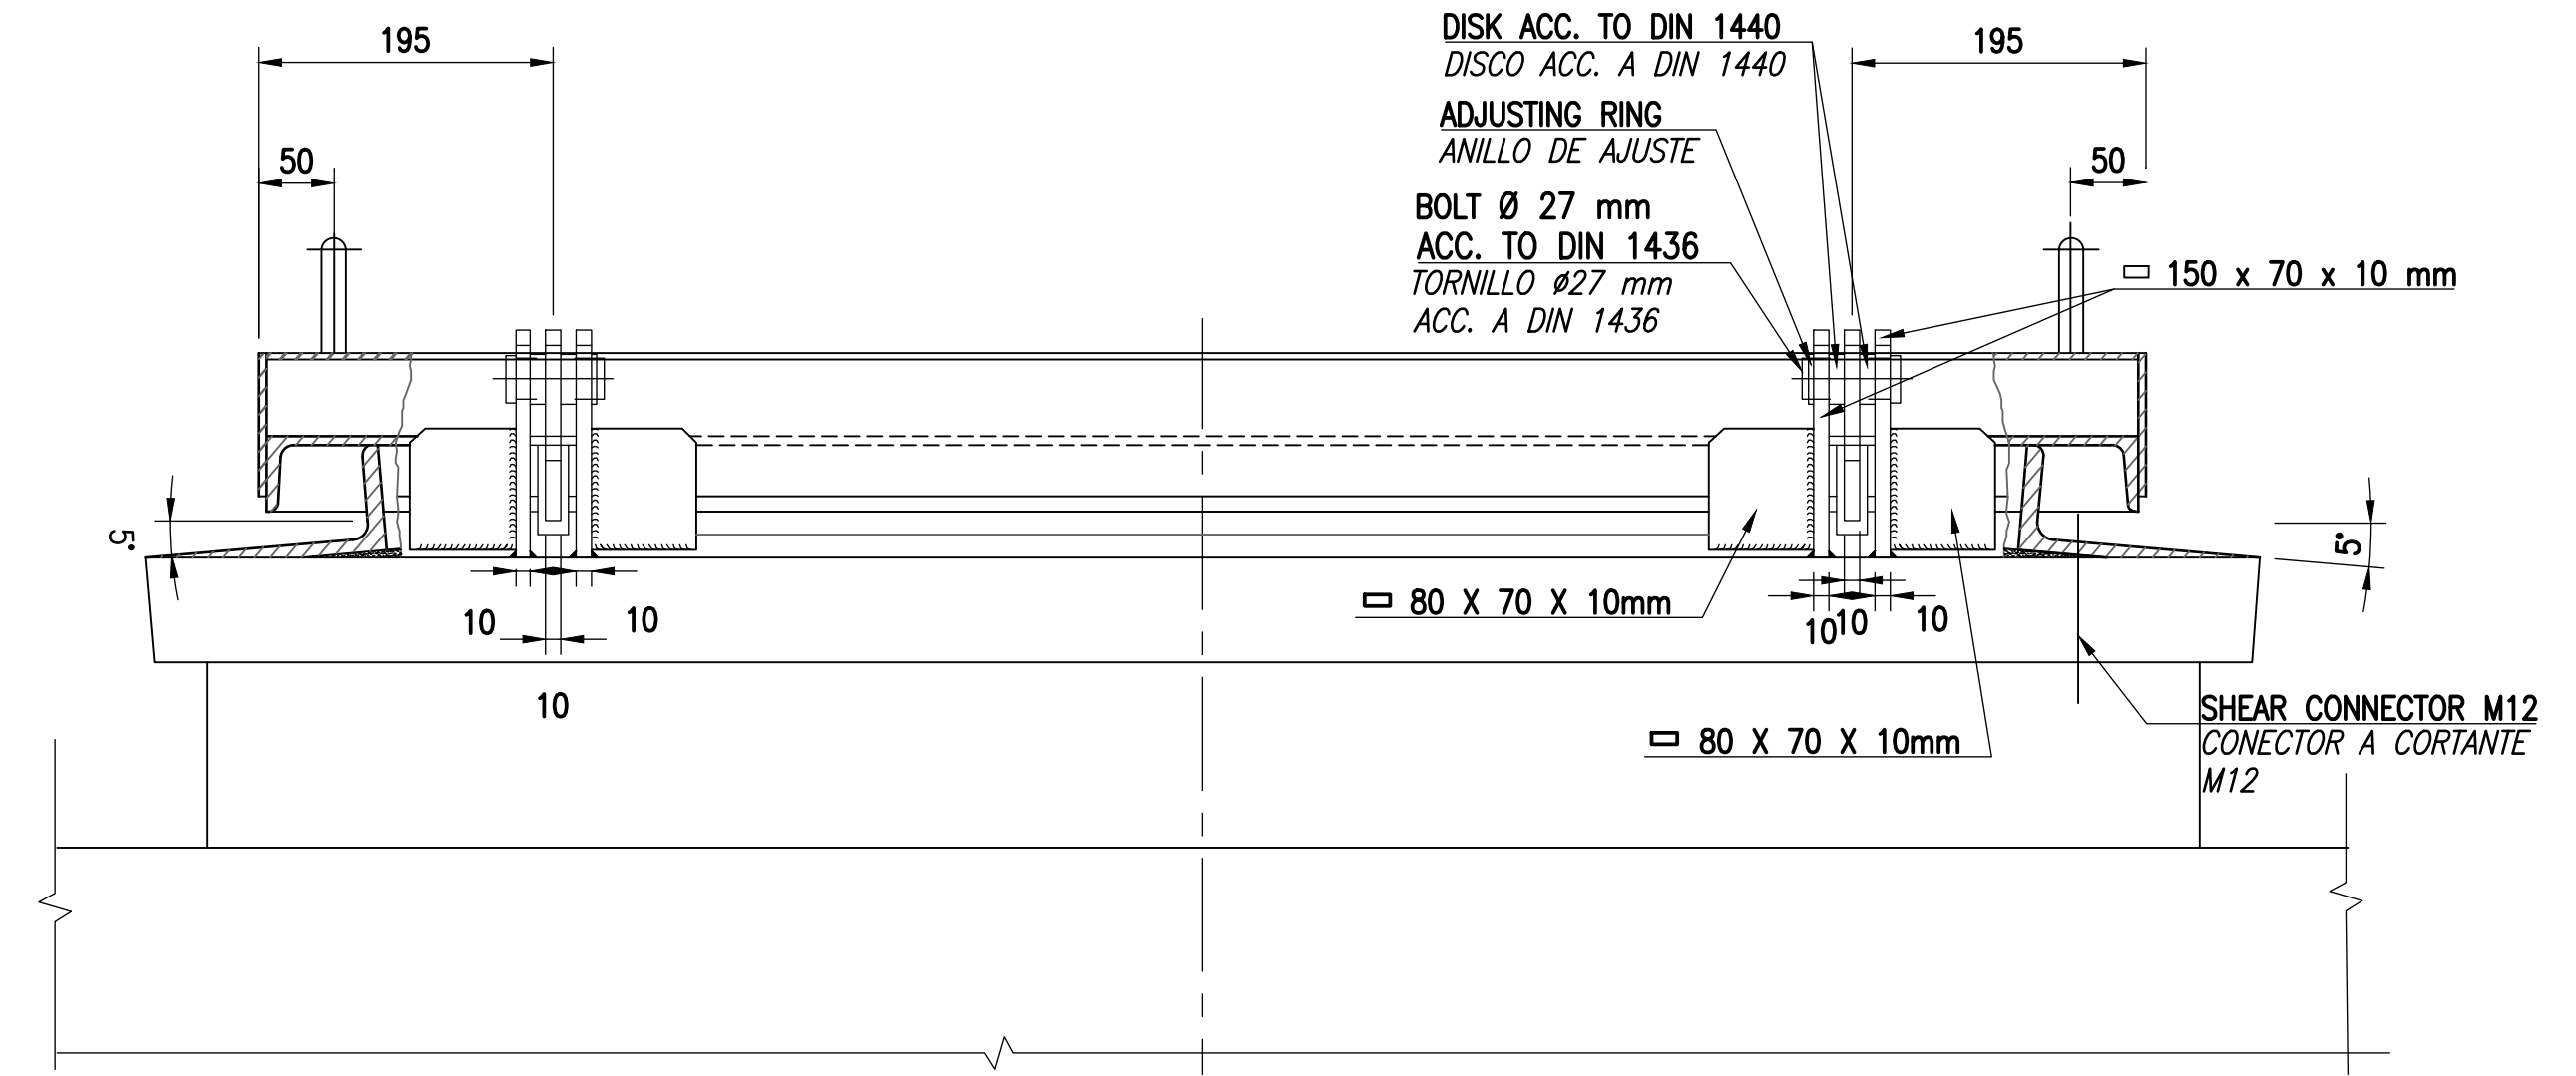

C4
SECTION
SECCIÓN
SCALE: 1:5
ESCALA: 1:5

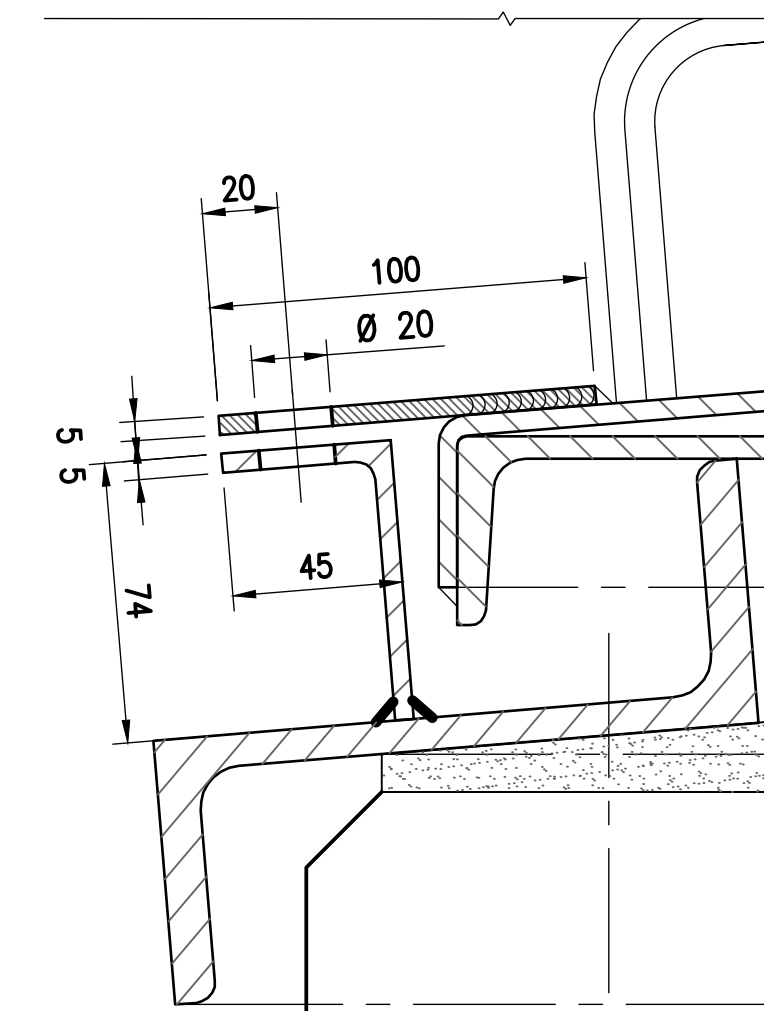

A4
DETAIL
DETALLE
SCALE: 1:2
ESCALA: 1:2

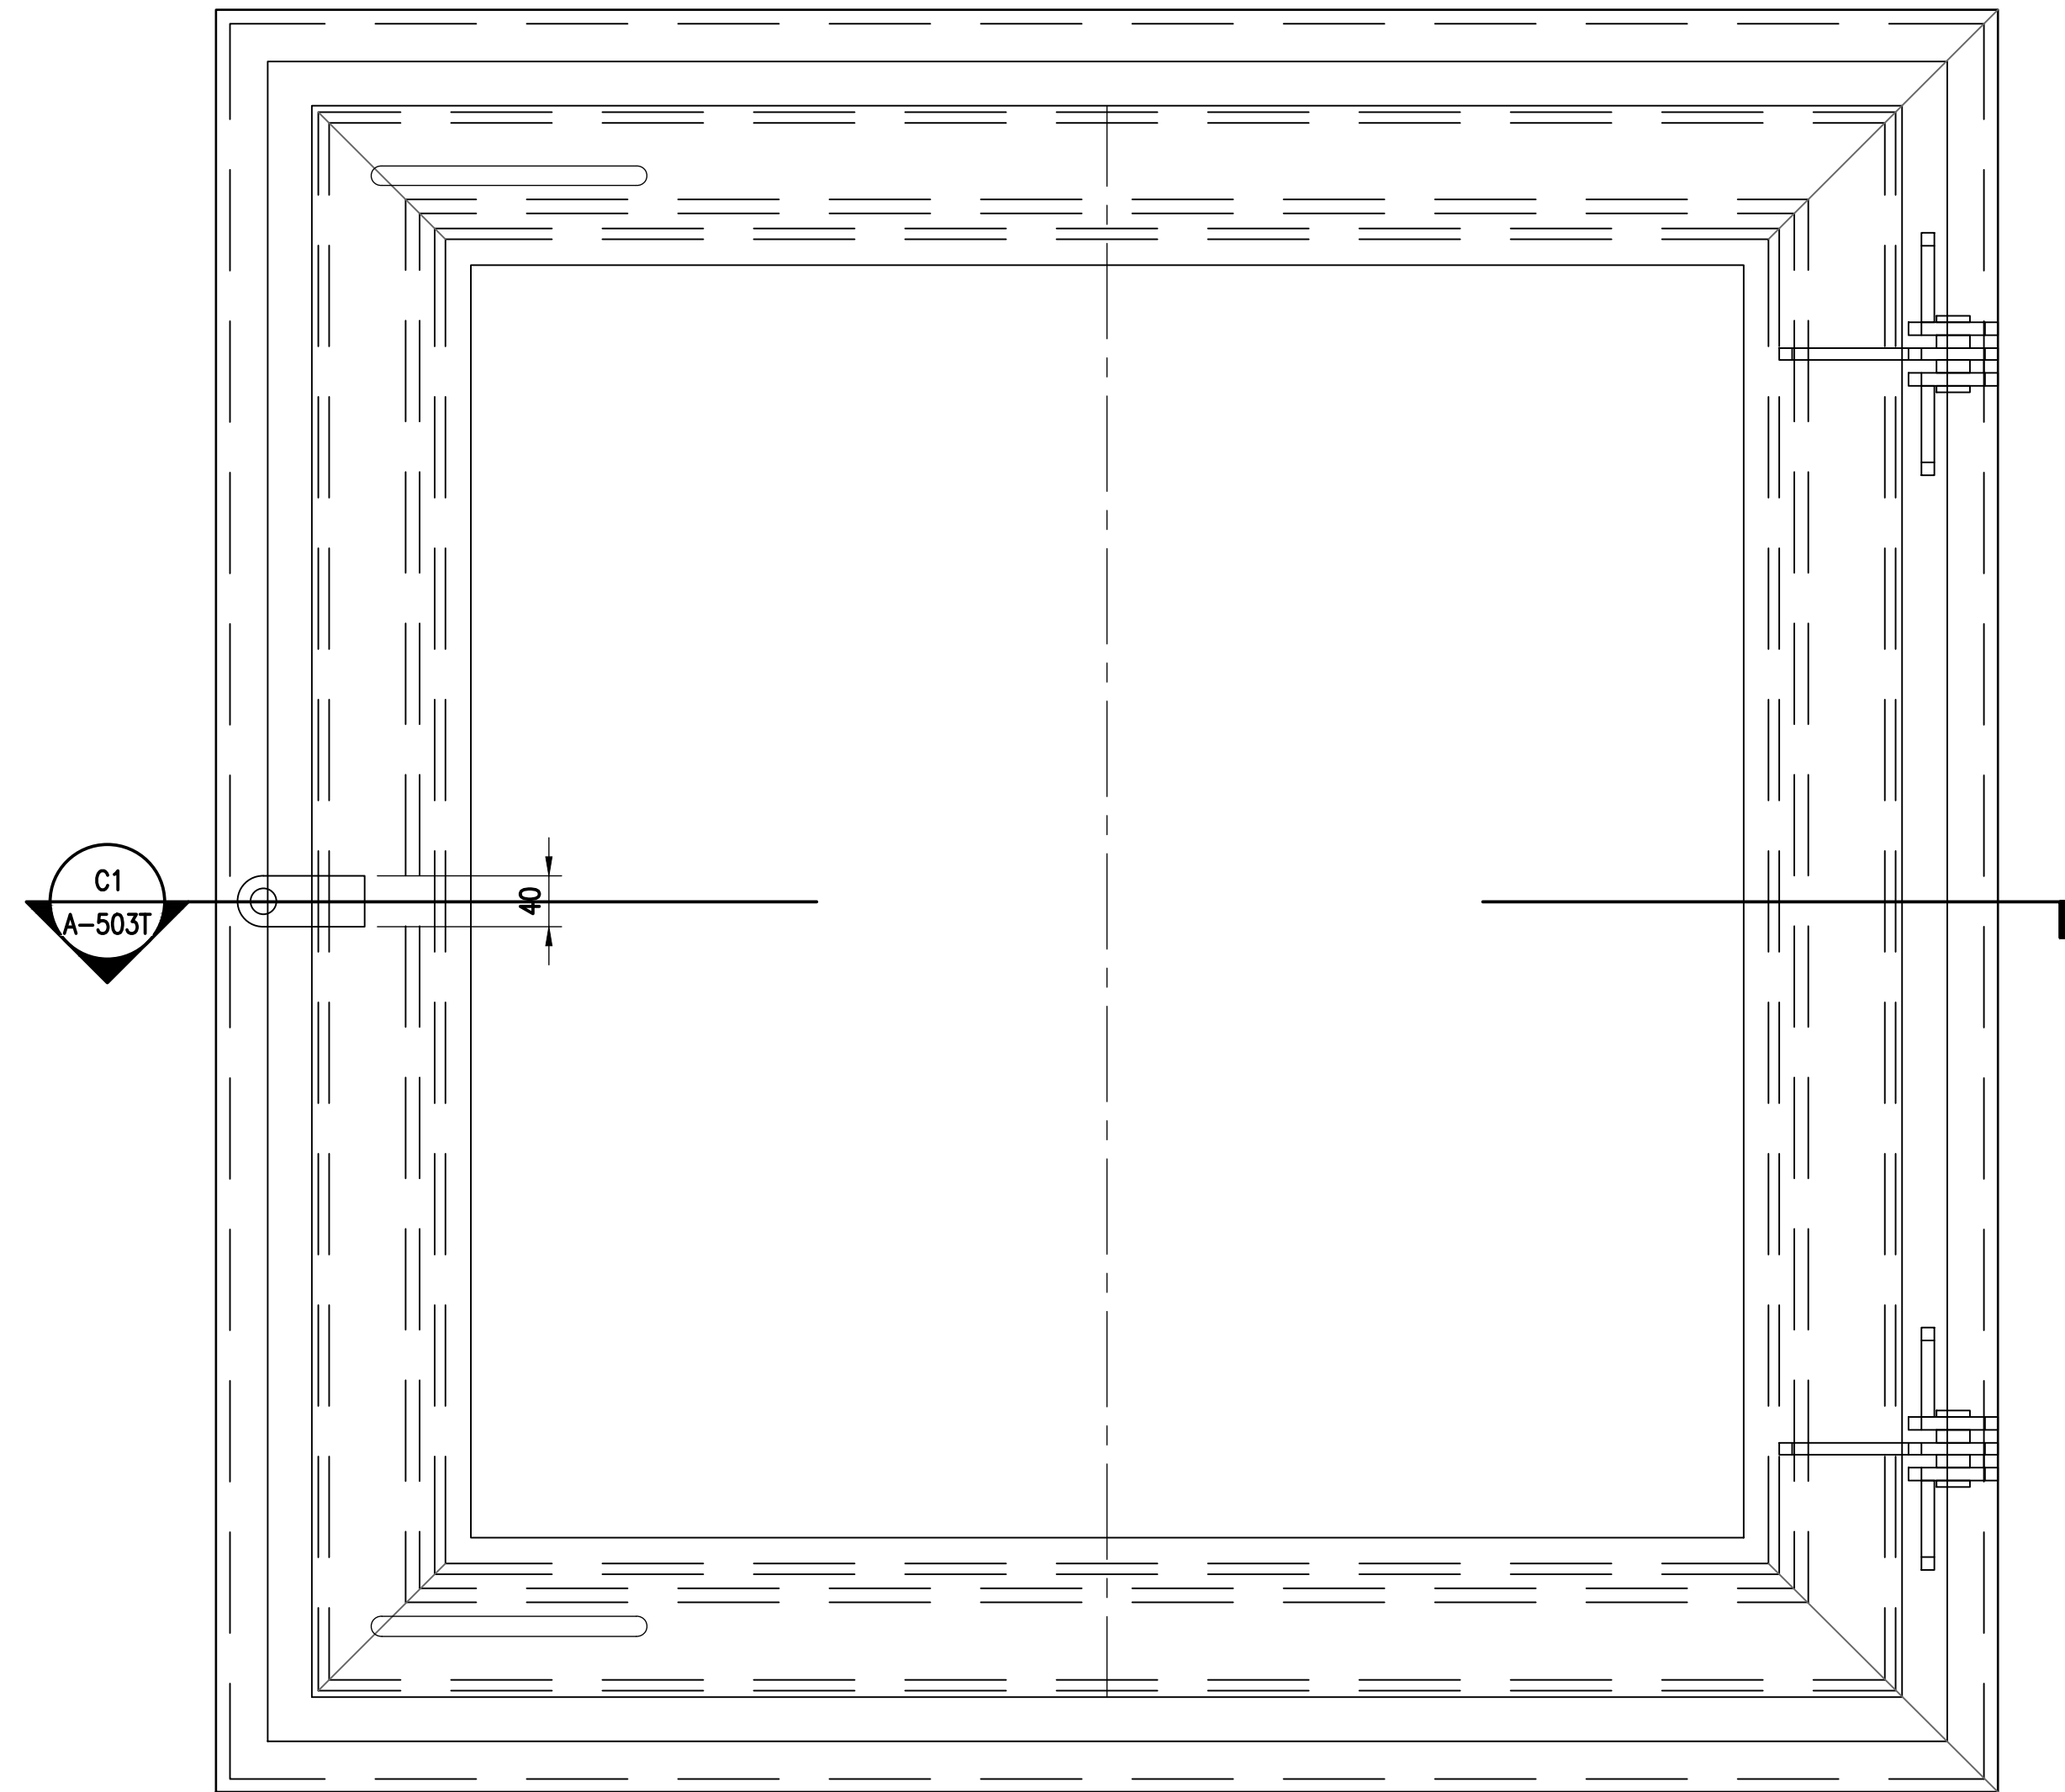

A1
PLAN VIEW
VISTA EN PLANTA
SCALE: 1:5
ESCALA: 1:5

GRAPHIC SCALE(S):
ESCALA(S) GRÁFICA(S):

0 50 100 200 500 mm
1:5

APPROVED	DATE	APPROVED
DESCRIPTION		
SYN		
NAVFAC		
COMMONWEALTH OF VIRGINIA		
SE JIN KWAK		
Lic. No. 014889		
ARCHITECT		
Brockenbrough		
ENGINEERING & CONSTRUCTION		
1011 Boulder Springs Drive, Suite 200, Chesapeake, Virginia 23026		
(804) 550-2500 (fax) (804) 550-2501 (cell)		
www.brockenbrough.com		
Stanley Consultants Inc.		
225 Iowa Avenue, Muscatine, Iowa 52761-3764		
www.stanleyconsultants.com		
APPROVED		
FOR COMMANDER NAVFAC		
ACTIVITY		
SATISFACTORY TO: DATE		
DES	CHK	CHK
PM/CM	CC/EA	CC/EA
BRANCH MANAGER		
DESIGN MANAGER		
FIRE PROTECTION		
XXX		
DEPARTMENT OF THE NAVY		
NAVAL FACILITIES ENGINEERING SYSTEM COMMAND		
NAVAL FACILITIES ENGINEERING SYSTEM COMMAND ~ ATLANTIC		
ATLANTIC DESIGN AND CONSTRUCTION		
NAVAL STATION ROTA		
P-919 BULK TANK FARM IMPROVEMENTS, PHASE 1		
DETAILS		
DETAILS		
SCALE:		
PROJECT NO.:		
CONSTR. CONTR. NO.:		
NAVFAC DRAWING NO.:		
14140172		
SHEET		
68 OF 342		
A-504T		
NAVFAC METRIC DRAWING REVISION: 07 AUGUST 2018		


FILE NAME: G:\21 Jobs\21-015 FY 23 MILCON P-919 Bulk Tanks - Rota\CDAVA-A-505 DETAILS (WINDOW & LOUVER) PLOTTED: Wednesday, July 03, 2024 -- 10:16am USER: mgpkins

D

C


B

A

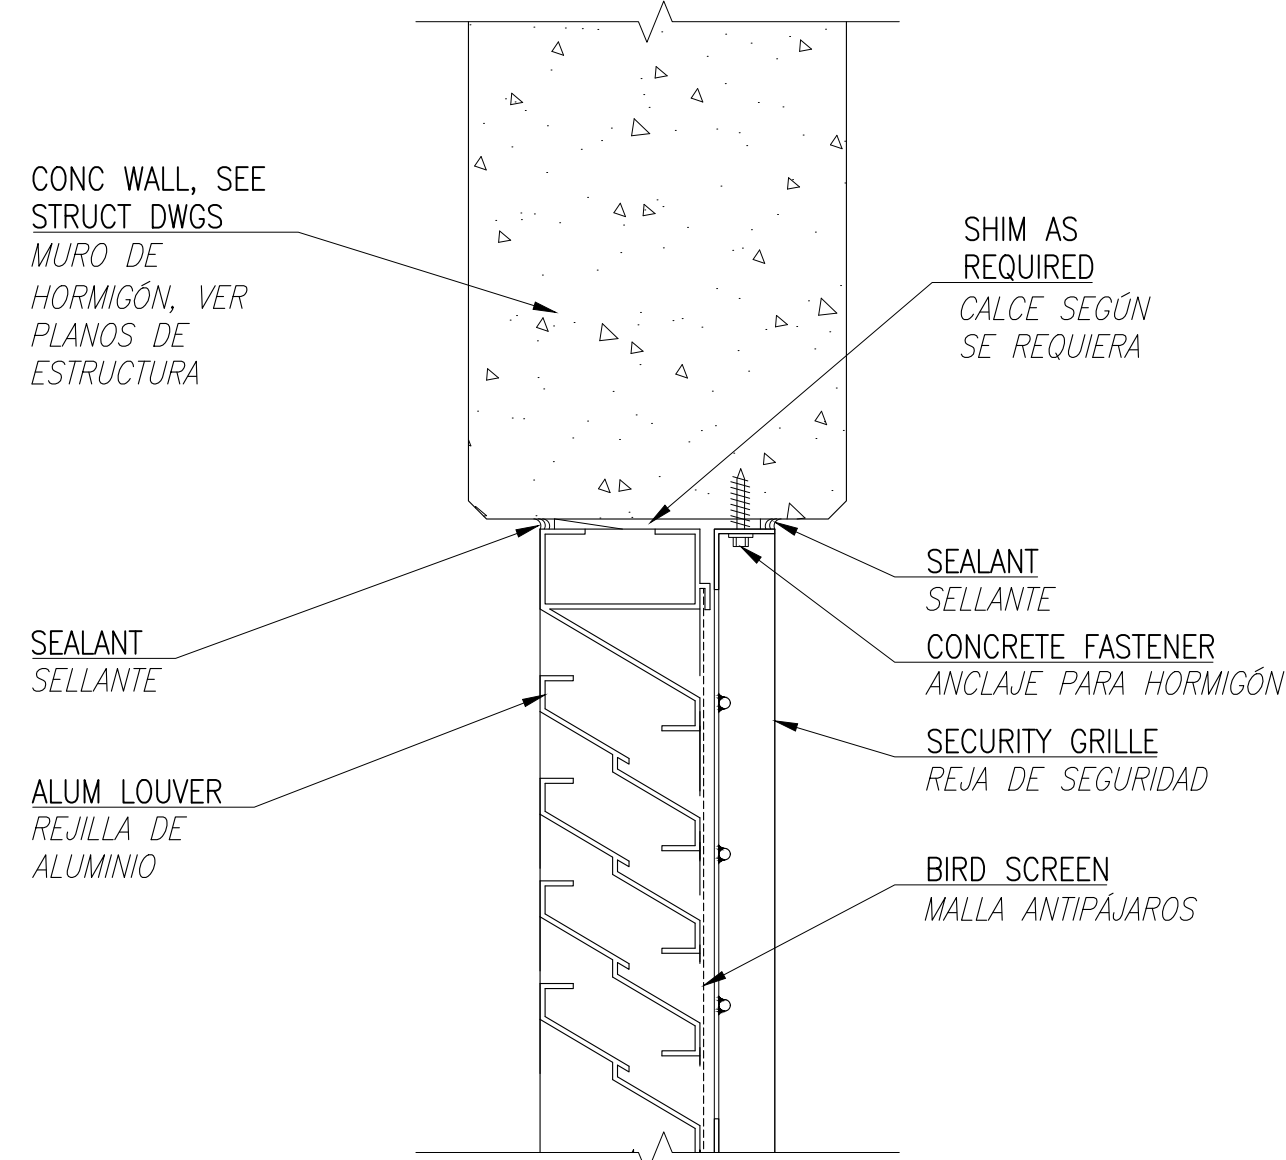

LOUVER DETAIL
DETALLE DE REJILLA

D1
SCALE: 1:5
ESCALA: 1:5

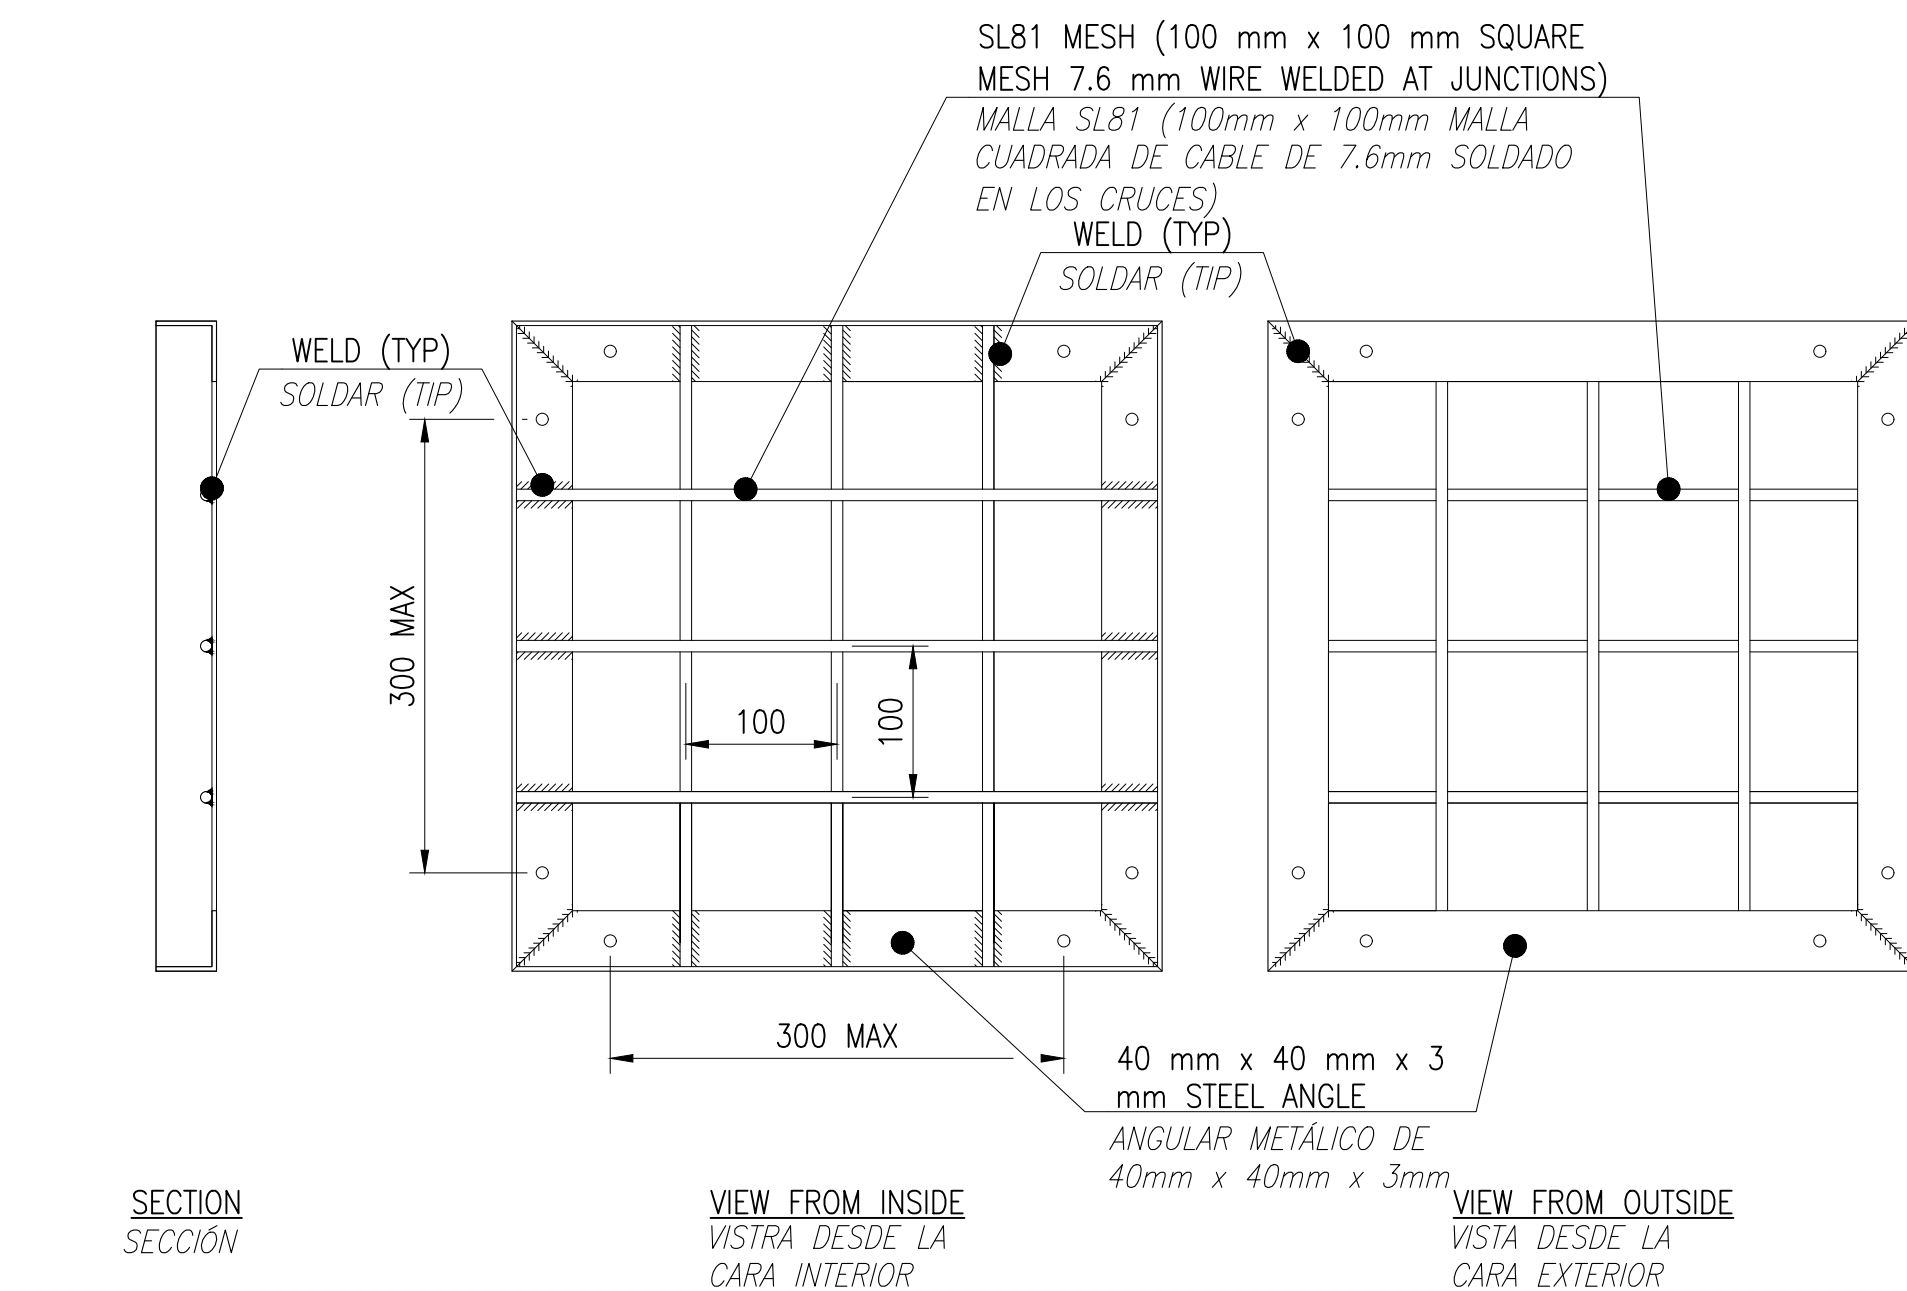


SECURITY GRILLE DETAIL
DETALLE DE REJA DE SEGURIDAD

A1
SCALE: 1:5
ESCALA: 1:5


NOTES: / NOTAS:

- GRILLE TO BE FASTENED TO THE STRUCTURE WITH TAMPER-EVIDENT FASTENERS ON A MAXIMUM SPACING OF 300mm.
LA REJILLA DEBE FIJARSE A LA ESTRUCTURA CON ANCLAJES ANTIMANIPULACIÓN CON UN ESPACIAMIENTO MÁXIMO DE 300mm.
- MATERIALS TO BE MILD STEEL.
LOS MATERIALES SERÁN DE ACERO DULCE.
- FASTENERS TO BE TUCK WELDED TO FRAME.
FIJACIONES PARA SOLDAR AL MARCO.

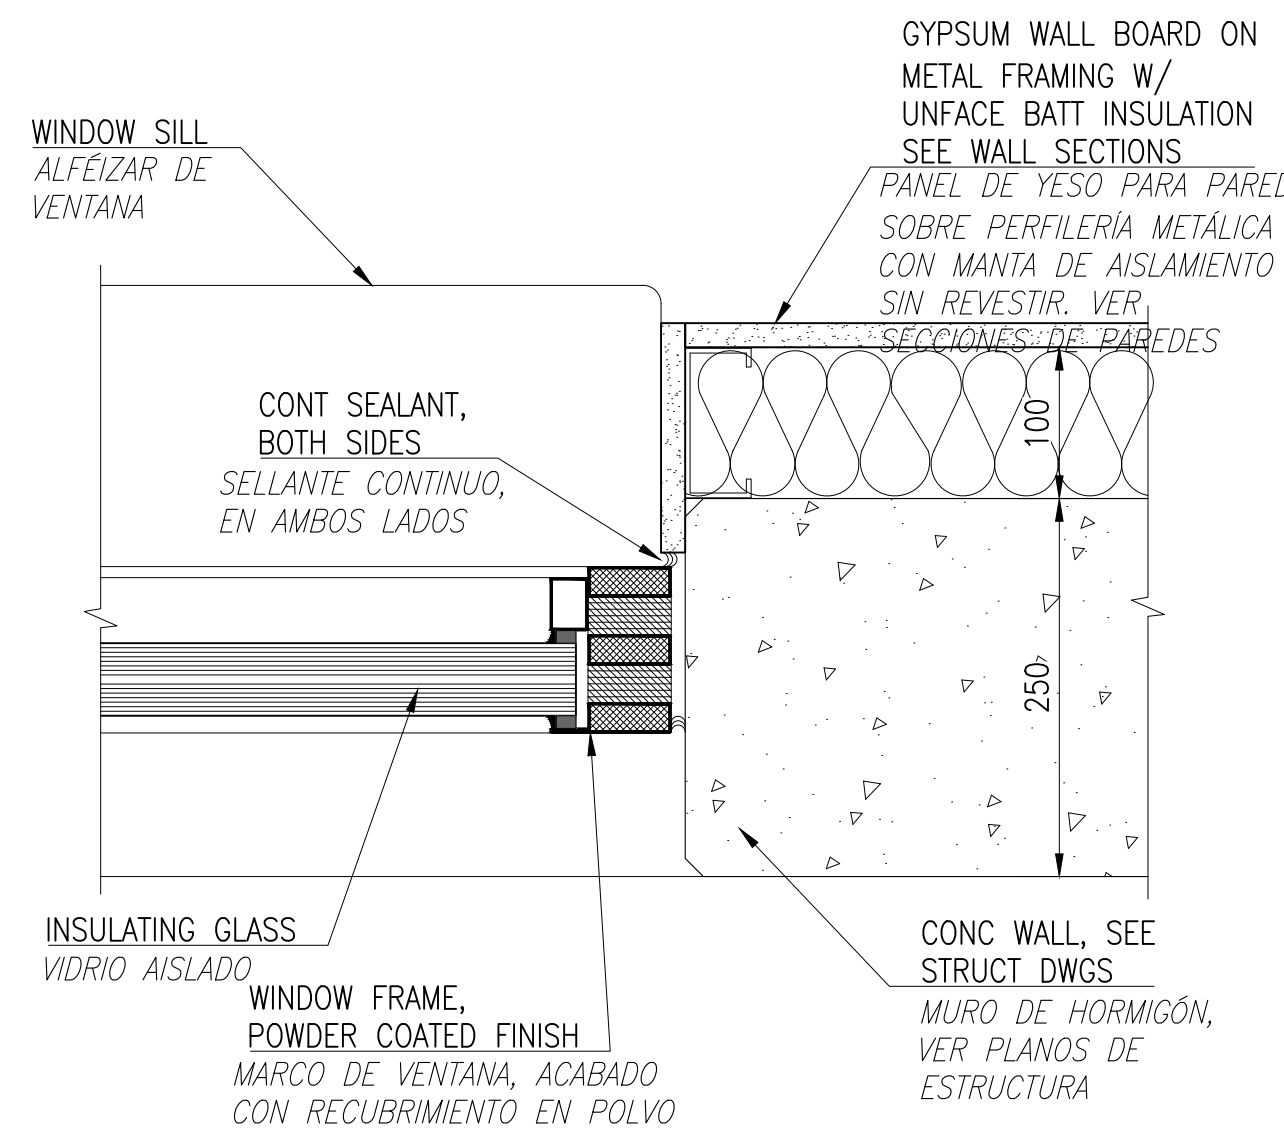

JAMB & HEAD DETAIL
DETALLE DE JAMBA Y DINTEL


D4
SCALE: 1:5
ESCALA: 1:5

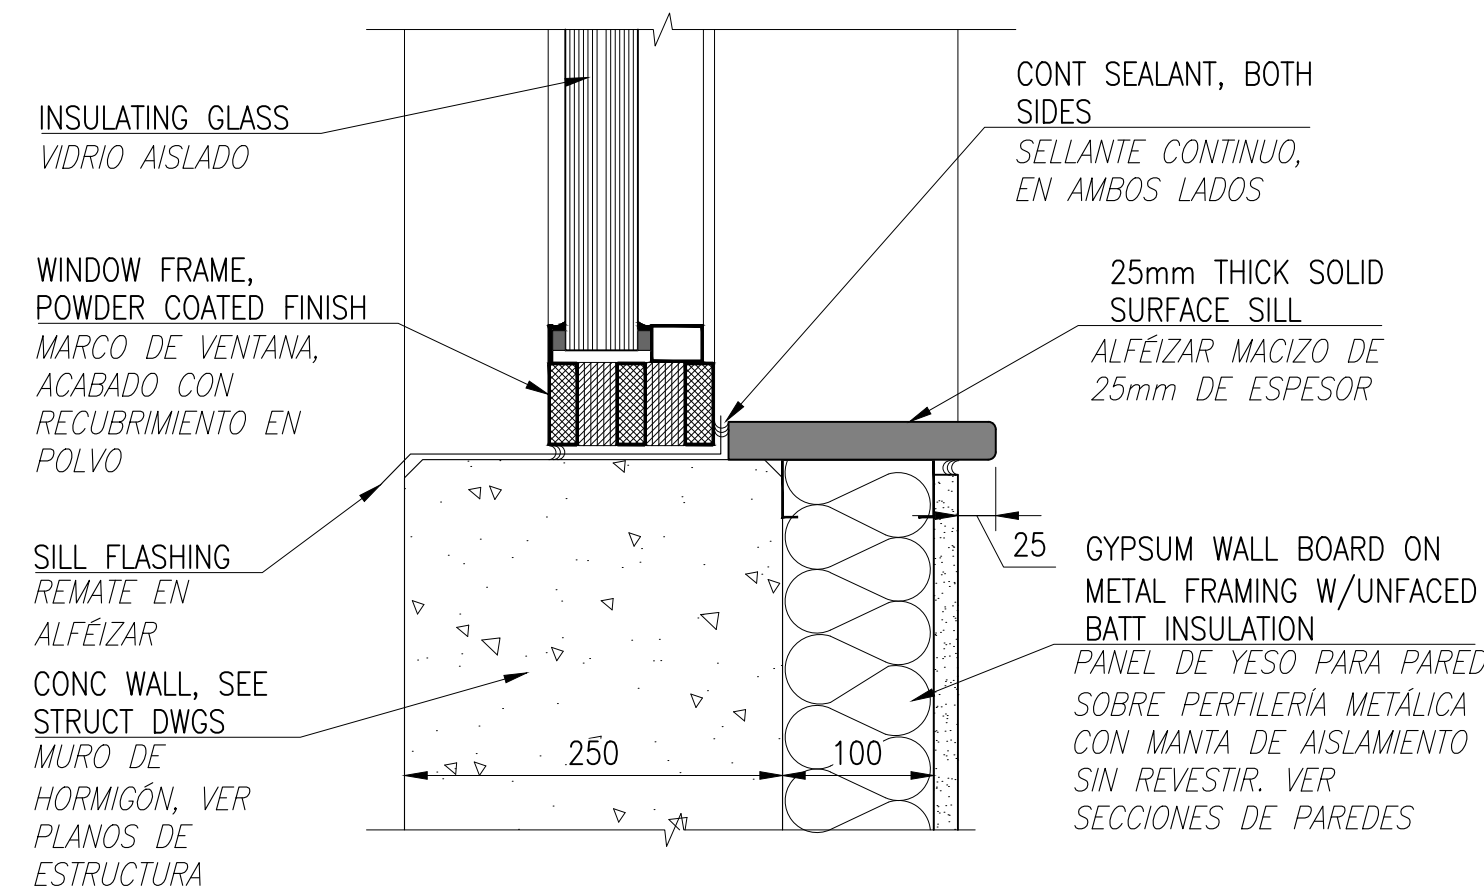

SILL DETAIL
DETALLE DE ALFÉIZAR

B4
SCALE: 1:5
ESCALA: 1:5

GRAPHIC SCALE(S):
ESCALA(S) GRÁFICA(S):

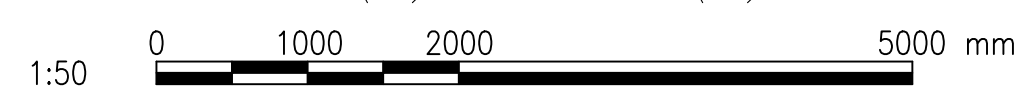


APPROVED	DATE	APPROVED
SYN	DESCRIPTION	SYN
SE JIN KWAK Lic. No. 014889 ARCHITECT		
225 West Avenue, Martinsville, Iowa 52761-3764 www.brockenbrough.com		
225 West Avenue, Martinsville, Iowa 52761-3764 www.stanleyconsultants.com		
APPROVED		
FOR COMMANDER NAVFAC		
ACTIVITY		
SATISFACTORY TO		
DES	SJK	DRW
PM/DM	SJK	CHK
BRANCH MANAGER	CC/EA	KWH
DESIGN MANAGER		
FIRE PROTECTION		XXX
NAVAL FACILITIES ENGINEERING SYSTEM COMMAND		
NAVAL FACILITIES ENGINEERING SYSTEM COMMAND ~ ATLANTIC		
NAVAL STATION ROTA		
P-919 BULK TANK FARM IMPROVEMENTS, PHASE 1		
DETAILS		
CUADROS		
SCALE:		
EPROJECT NO.:		
CONSTR. CONTR. NO.:		
NAVFAC DRAWING NO.:		
14140173		
SHEET		
69 of 342		
A-505T		

D

C

B

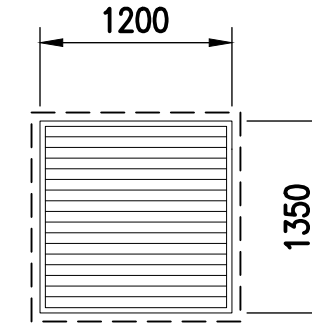A

LOUVER 2
REJILLA 2

NOTE: SEE A505T FOR DETAILS
NOTA: VER A505T PARA DETALLES

A3

A4

1:50



5

 Δ 5

ROOM HABITACIÓN		FLOOR SUELO	BASE RODAPIE	WALLS PAREDES		CEILINGS TECHOS		SEE NUMBERED NOTES BELOW VER NOTAS ENUMERADAS DEBAJO
NUMBER NÚMERO	NAME NOMBRE			MATERIAL	FINISH ACABADO	MATERIAL	HEIGHT ACABADO	
300	EQUIPMENT ROOM CUARTO DE EQUIPOS	CONC HORM.	—	CONC HORMIGÓN	---	CONC HORMIGÓN	—	
301	ELECTRICAL ROOM CUARTO ELÉCTRICO	AFS/ SCF	RB GOMA	GYP BD PANEL YESO	PNTD PINTADO	ACP LOSETA AC.	2450	

NOTES:

- ALL EXPOSED CONCRETE FLOORS TO BE SEALED WITH CONCRETE SEALER.
- EXTEND SEALER UP EQUIPMENT ROOM WALLS 600 mm.

NOTAS:

- TODOS LOS SUELOS EXPUESTOS DE HORMIGÓN IRÁN SELLADOS CON SELLADOR PARA HORMIGÓN.
- EXTENDER EL SELLADOR POR ENCIMA DE LAS PAREDES DEL CUARTO DE EQUIPOS 600mm.

<u>ABBREVIATIONS</u> / <u>ABREVIATURAS</u>	
ACP	ACOUSTIC CEILING PANELS <i>LOSETAS ACÚSTICAS PARA TECHO</i>
AFS	ACCESS FLOOR SYSTEM <i>SISTEMA DE SUELO REGISTRABLE</i>
CONC	CONCRETE (UNPAINTED) <i>HORMIGÓN (SIN PINTAR)</i>
GYP BD	GYPSUM BOARD <i>PANEL DE YESO</i>
PNTD	PAINTED <i>PINTADO</i>
RB	RUBBER BASE <i>RODAPIÉ DE GOMA</i>
SCF	STATIC-CONTROL FLOORING <i>SUELO CON CONTROL ESTÁTICO</i>