




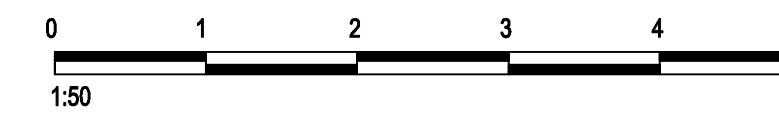


- △

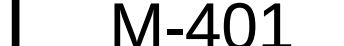

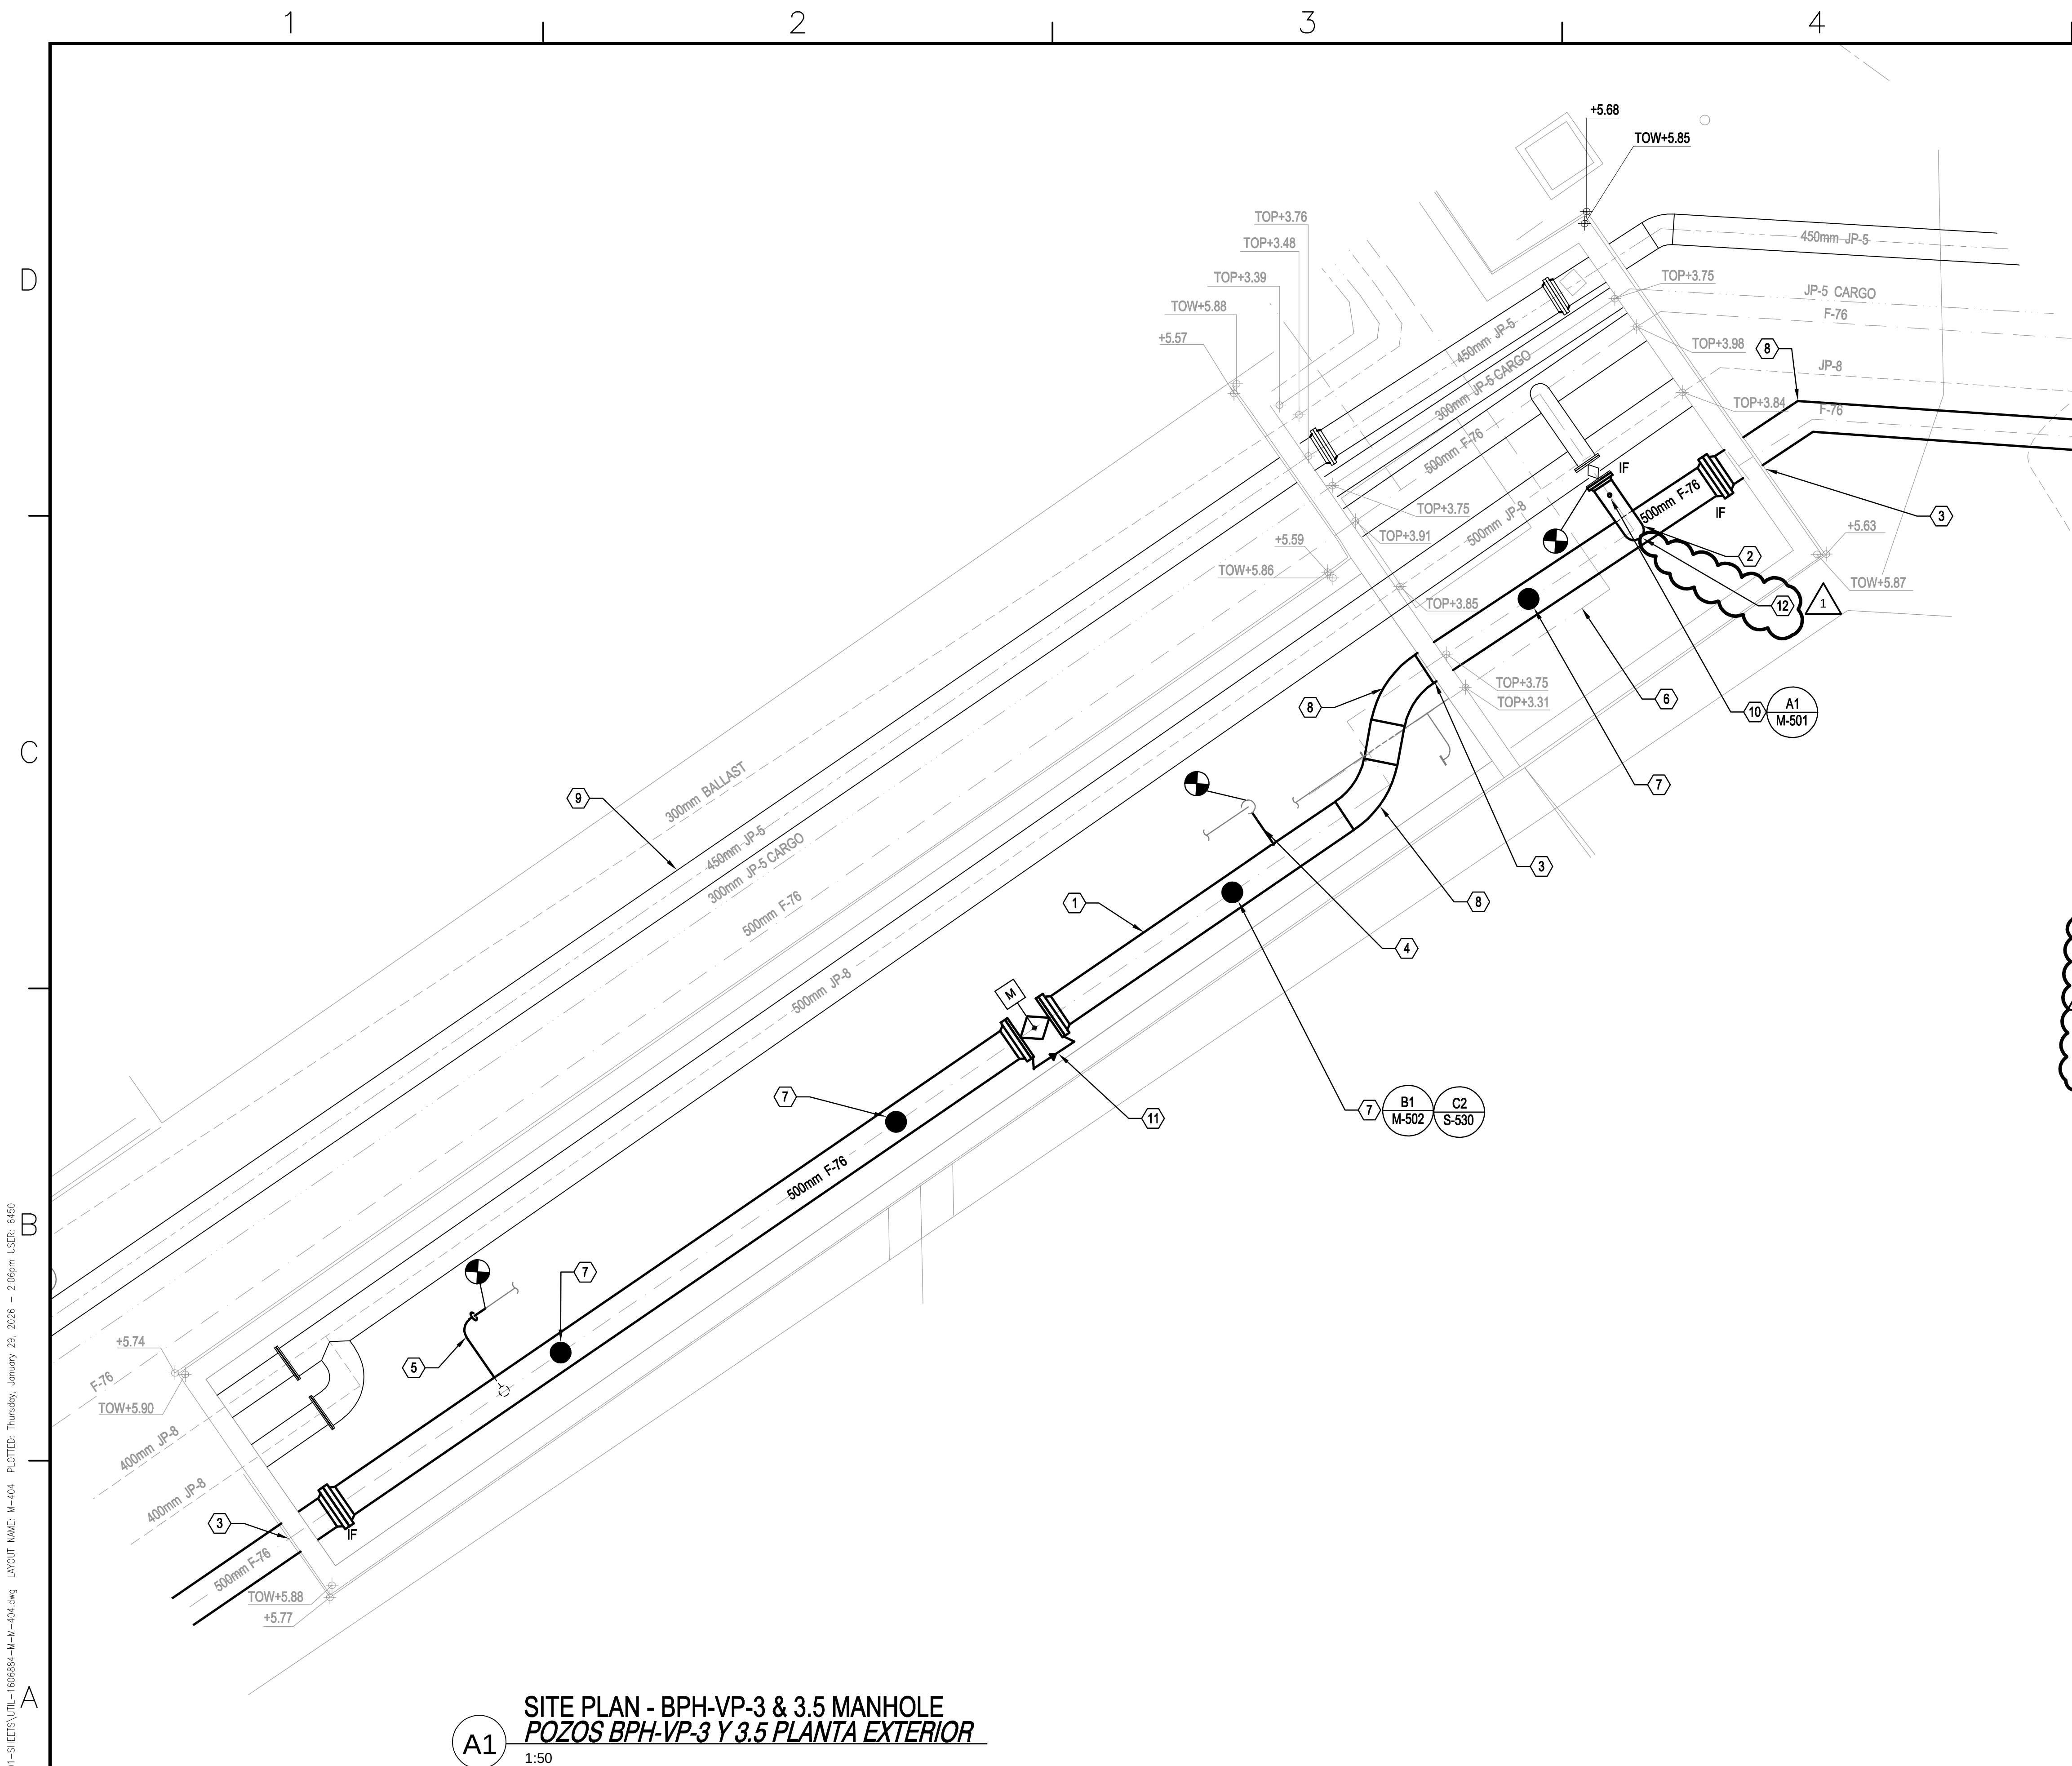


SITE PLAN - BPH-VP-3 & 3.5 MANHOLE
POZOS BPH-VP-3 Y 3.5 PLANTA EXTERIOR

- ## KEYED NOTES:
- ### NOTAS DE REFERENCIA:
1. PROVIDE 500mm F-76 PIPE. PROVIDE ONE PIPE DIAMETER (500mm) CLEARANCE BETWEEN PIPE WALLS IN ACCORDANCE WITH UFC 3-460-01
 1. *PROVEER TUBERÍA F-76 DE 500mm. PROVEER UN DIÁMETRO DE TUBERÍA (500mm) DE DISTANCIA LIBRE ENTRE LAS PAREDES DE LA TUBERÍA DE ACUERDO A LA UFC 3-460-01.*
 2. 300mm F-76
 2. *F-76 DE 300mm.*
 3. ENLARGE PENETRATION TO INSTALL 500mm PIPE. FILL IN EXISTING PENETRATIONS AND REHABILITATE DAMAGED CONCRETE IN ACCORDANCE WITH SPECIFICATION 03 01 00 AND ACI 562-16
 3. *AMPLIAR LA PENETRACIÓN PARA INSTALAR LA TUBERÍA DE 500mm. RELLENAR LAS PENETRACIONES EXISTENTES Y REPARAR EL HORMIGÓN DAÑADO DE ACUERDO A LA ESPECIFICACIÓN 03 01 00 Y ACI 562-16.*
 4. 100mm DISCHARGE FROM PUMP P-1.
 4. *DESCARGA DE 100mm DESDE LA BOMBA P-1.*
 5. 100mm SUCTION CONNECTION FOR PUMP P-1.
 5. *CONEXIÓN DE SUCCIÓN DE 100mm PARA LA BOMBA P-1.*
 6. 200mm F-76.
 6. *F-76 DE 200mm.*
 7. FREE PIPE SUPPORT
 7. *SOPORTE DE TUBERÍA LIBRE*
 8. PROVIDE 3 DIAMETER BEND RADIUS ELBOW
 8. *PROVEER UN CODO DE RADIO DE CURVATURA DE 3 DIÁMETRO*
 9. 450 mm JP-5 LINE TO BE INSTALLED UNDER ANOTHER CONTRACT. CONTACT ROTA PUBLIC WORKS FOR THE CONSTRUCTION SCHEDULE.
 9. *TUBERÍA JP-5 DE 450mm A SER INSTALADA BAJO OTRO CONTRATO. CONTACTAR CON OBRAS PÚBLICAS EN ROTA PARA EL PROGRAMA DE CONSTRUCCIÓN.*
 10. PROVIDE HIGH-POINT VENT
 10. *PROVEER VENITEO EN PUNTO ALTO*
 11. PROVIDE FULL PORT DB&B PLUG VALVE (PIGGABLE) WITH THERMAL RELIEF.
 11. *PROVEER VALVULA OBTURADORA DE DOBLE BLOQUEO Y DRENAJE DE PASO COMPLETO (PIGABLE) CON ALIVIO TÉRMICO.*
 12. PROVIDE TEE WITH GUIDE BARS.
 12. *PROVEER TE CON BARRAS GUIA.*

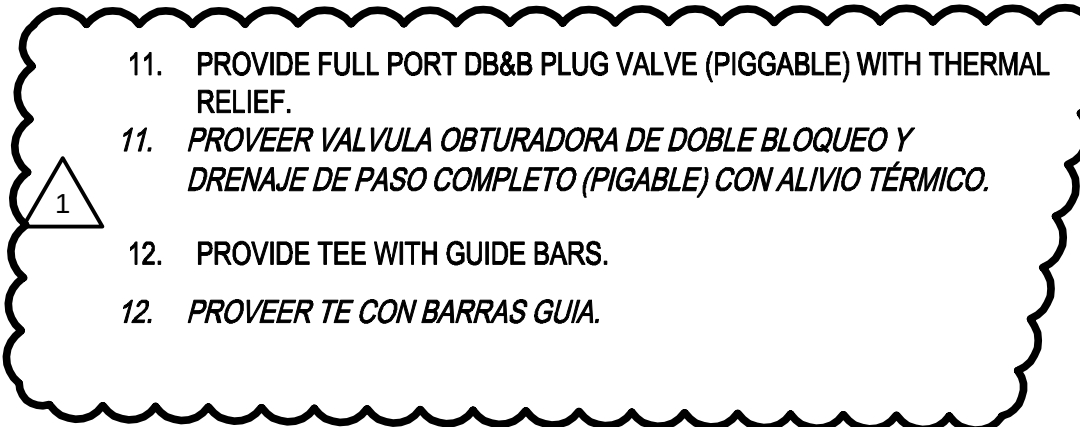

DEPARTMENT OF THE NAVY NAVAL FACILITIES ENGINEERING SYSTEM COMMAND NAVAL FACILITIES ENGINEERING SYSTEM COMMAND ~ ATLANTIC ATLANTIC DESIGN AND CONSTRUCTION		NAVAL FACILITIES ENGINEERING SYSTEM COMMAND NAVAL FACILITIES ENGINEERING SYSTEM COMMAND ~ ATLANTIC NORFOLK, VA		ROTTA, SPAIN		REPLACE		FUEL PIPELINE FROM PIER 3 TO BULK STORAGE		ENLARGED SITE PLAN BPH-VP- 3 & 3.5 MANHOLE PLANTA EXTERIOR - POZOS BPH-VP- 3 Y 3.5		SCALE: AS NOTED		PROJECT NO.: 1606884		CONSTR. CONTR. NO.		NAVFAC DRAWING NO. 14142801		SHEET 100 OF 149		M-404			
APPROVED:		FOR COMMANDER NAVFAC		ACTIVITY		SATISFACTORY TO		DATE		DES TAS		DRW CMR		CHK JV		PM/EM		DCA/EIL		BRANCH MANAGER		DESIGN MANAGER		FIRE PROTECTION	
225 Iowa Avenue, Muscatine, Iowa 52761-3764 www.starlineconsultants.com		A/E INFO		SEAL		TIMOTHY A SCHMITT 17386		IOWA		NAVFAC		1		REVISED NOTE AND ADDED KEY NOTE		01-30-2026		TS		DATE		APPR			



FILE NAME: I:\231423\04-CIVIL\01-SHEETS\UTIL-1606884-M-M-410.dwg LAYOUT NAME: M-410 PLOTTED: Thursday, January 29, 2026 - 2:09pm USER: 6450

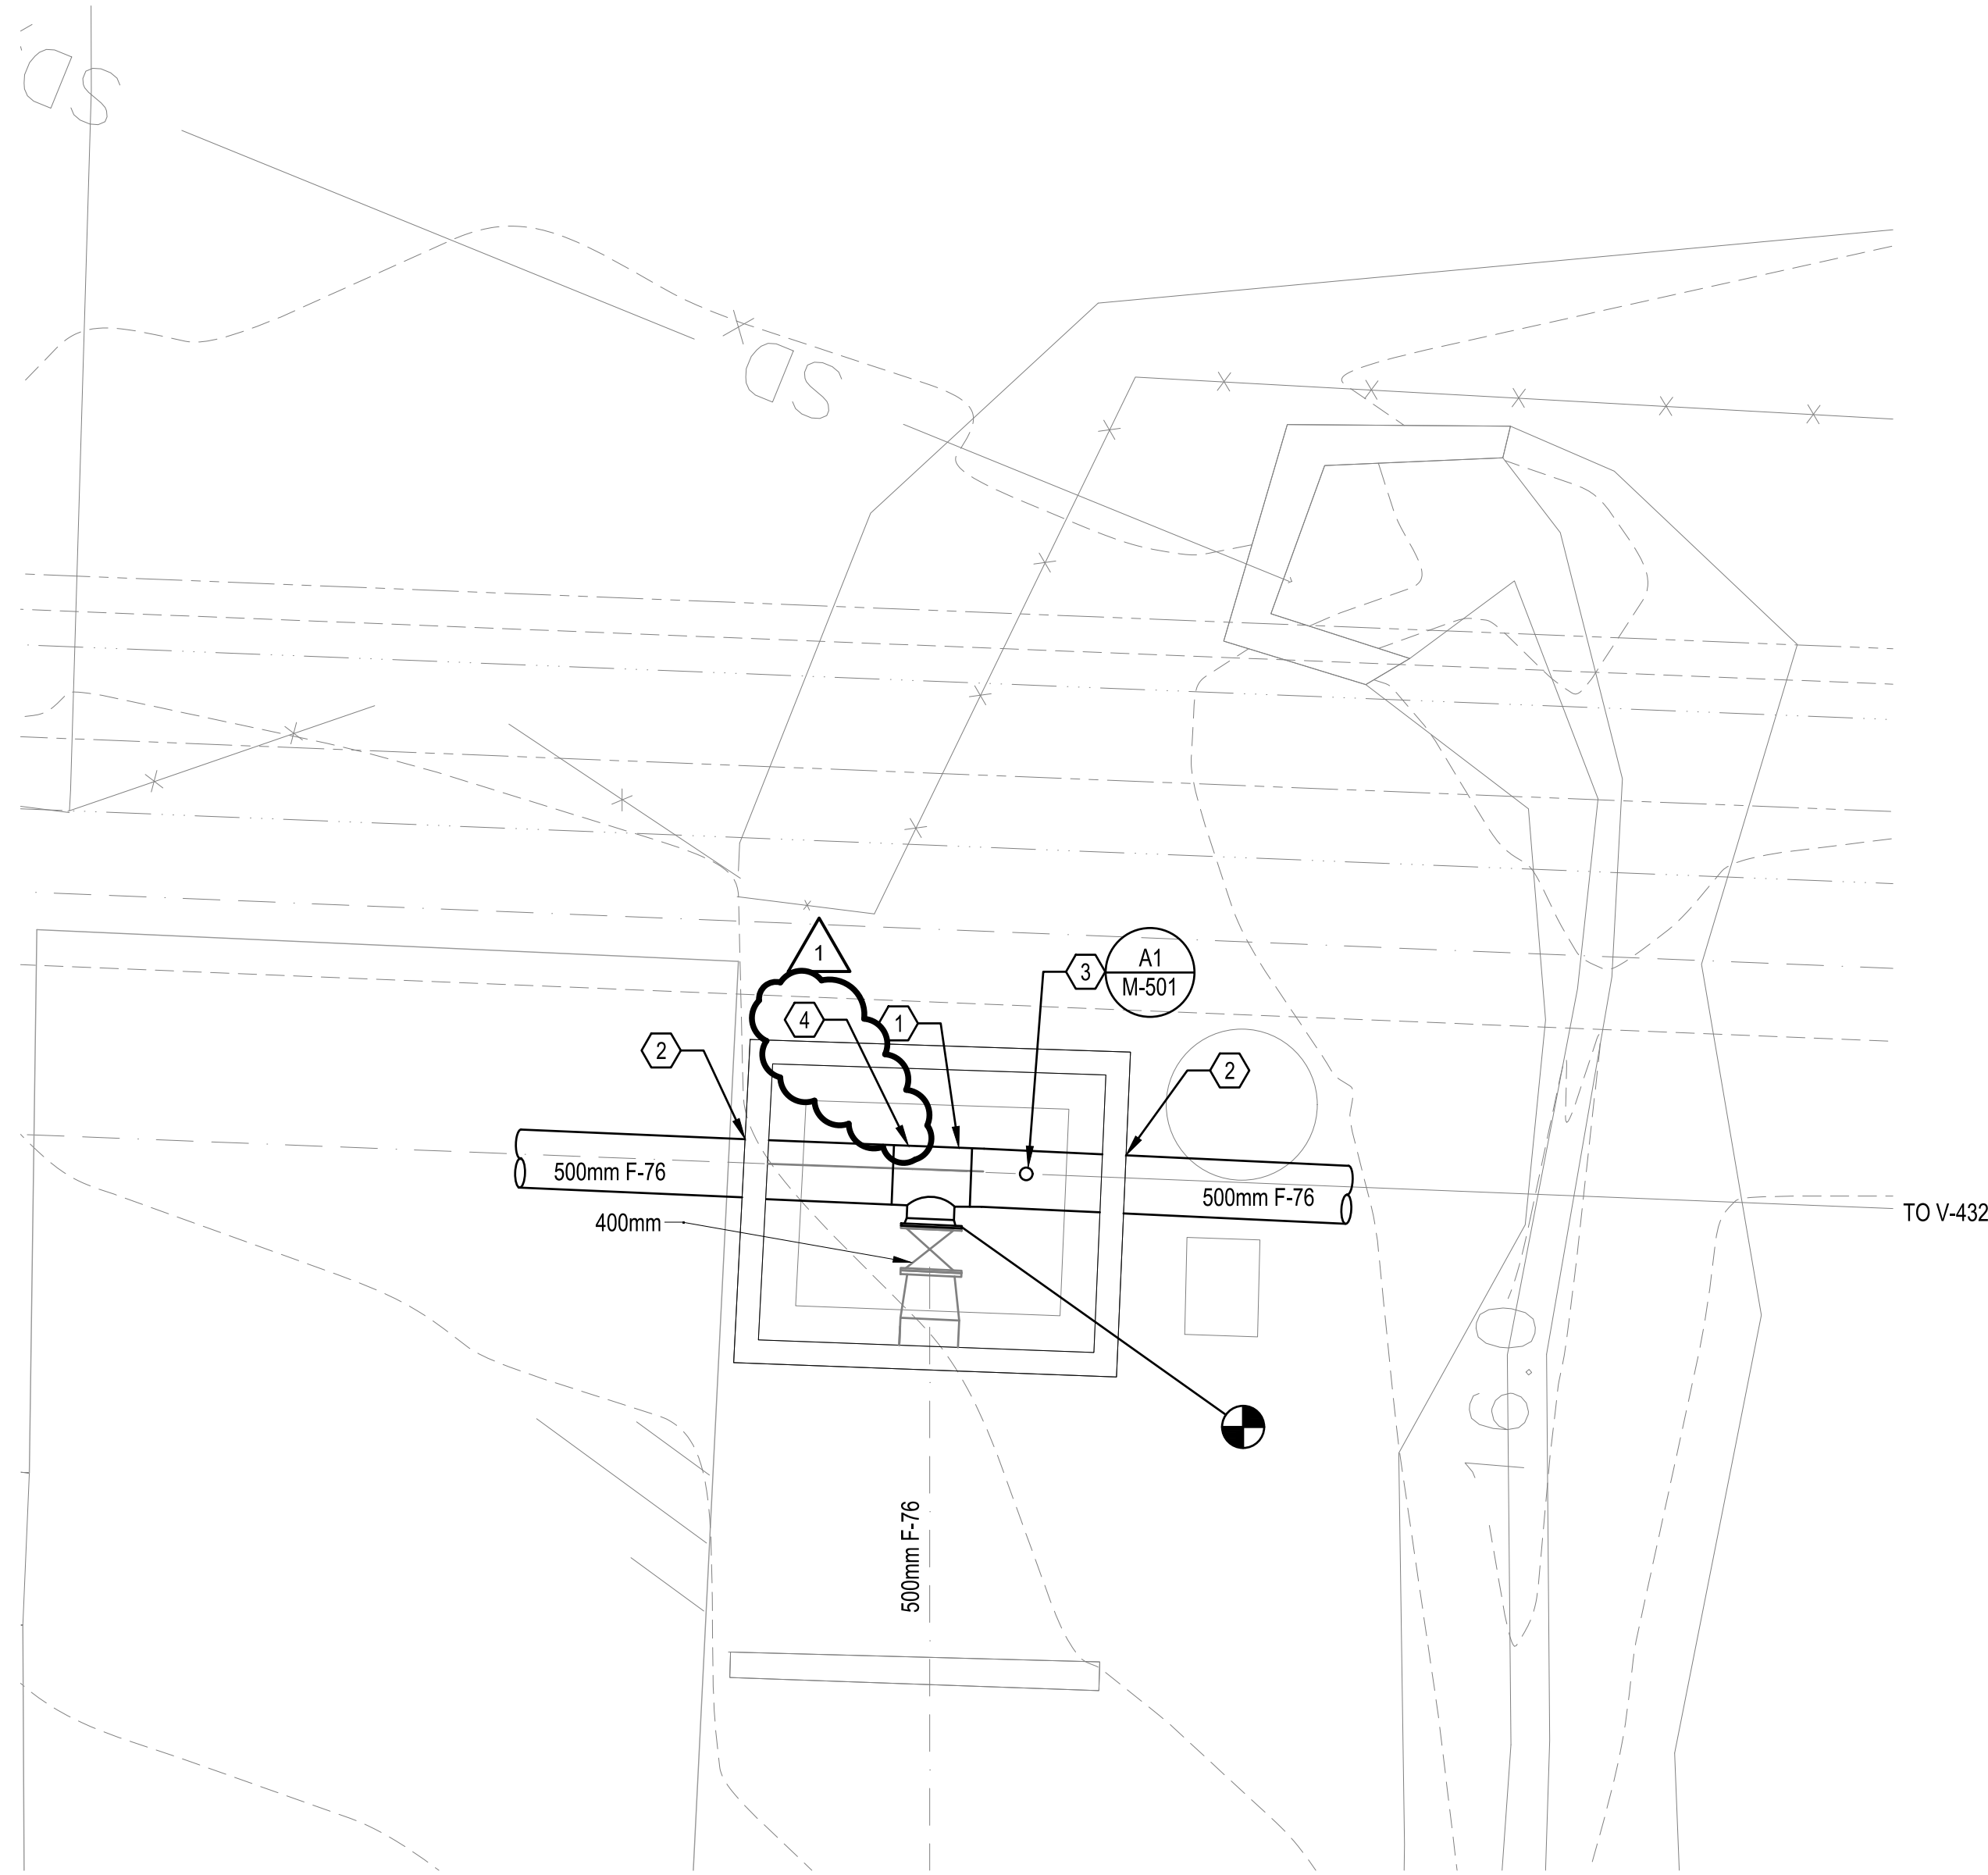

B1 PLAN - ML-1 MANHOLE
PLANTA - POZO ML-1
1:50

KEYED NOTES:
NOTAS DE REFERENCIA:

1. PROVIDE 500mm F-76.
1. PROVEER TUBERÍA F-76 DE 500mm.
2. REPAIR VALVE PIT WALL PENETRATION AROUND 500mm PIPE AS NEEDED. REHABILITATE DAMAGED CONCRETE IN ACCORDANCE WITH SPECIFICATION 03 01 00 AND ACI 562-16.
2. REPARAR LA PENETRACIÓN DE LA PARED DE LA FOSA PARA LA VÁLVULA ALREDEDOR DE LA TUBERÍA DE 500mm SEGÚN SE NECESITE. REPARAR EL HORMIGÓN DAÑADO DE ACUERDO A LA ESPECIFICACIÓN 03 01 00 Y ACI 562-16.
3. HIGH-POINT VENT.
3. VENTEO EN PUNTO ALTO
4. PROVIDE TEE WITH GUIDE BARS.
4. PROVEER TE CON BARRAS GUIA.

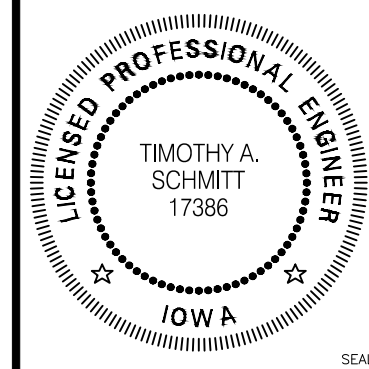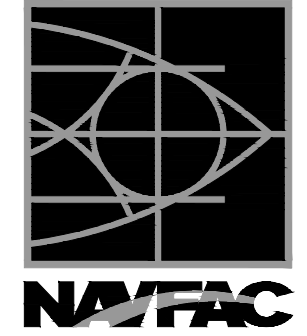

APPROVED

FOR COMMANDER NAVFAC

ACTIVITY

SATISFACTORY TO DATE

DES: TAS DRW: GMR CHK: JV

PM/DM: CCA/EAL

BRANCH MANAGER

DESIGN MANAGER

FIRE PROTECTION

SCALE: AS NOTED

PROJECT NO.: 1606884

CONSTR. CONTR. NO.


NAVFAC DRAWING NO. 14142802

SHEET 101 OF 149

M-410

NAVFAC METRIC DRAWING REVISION: 07 AUGUST 2018


FILE NAME: I:\2317423\04-CIVIL\01-SHEETS\UTIL-1606884-M-M-411.dwg LAYOUT NAME: M-411 PLOTTED: Wednesday, January 28, 2026 - 12:05pm USER: 6450

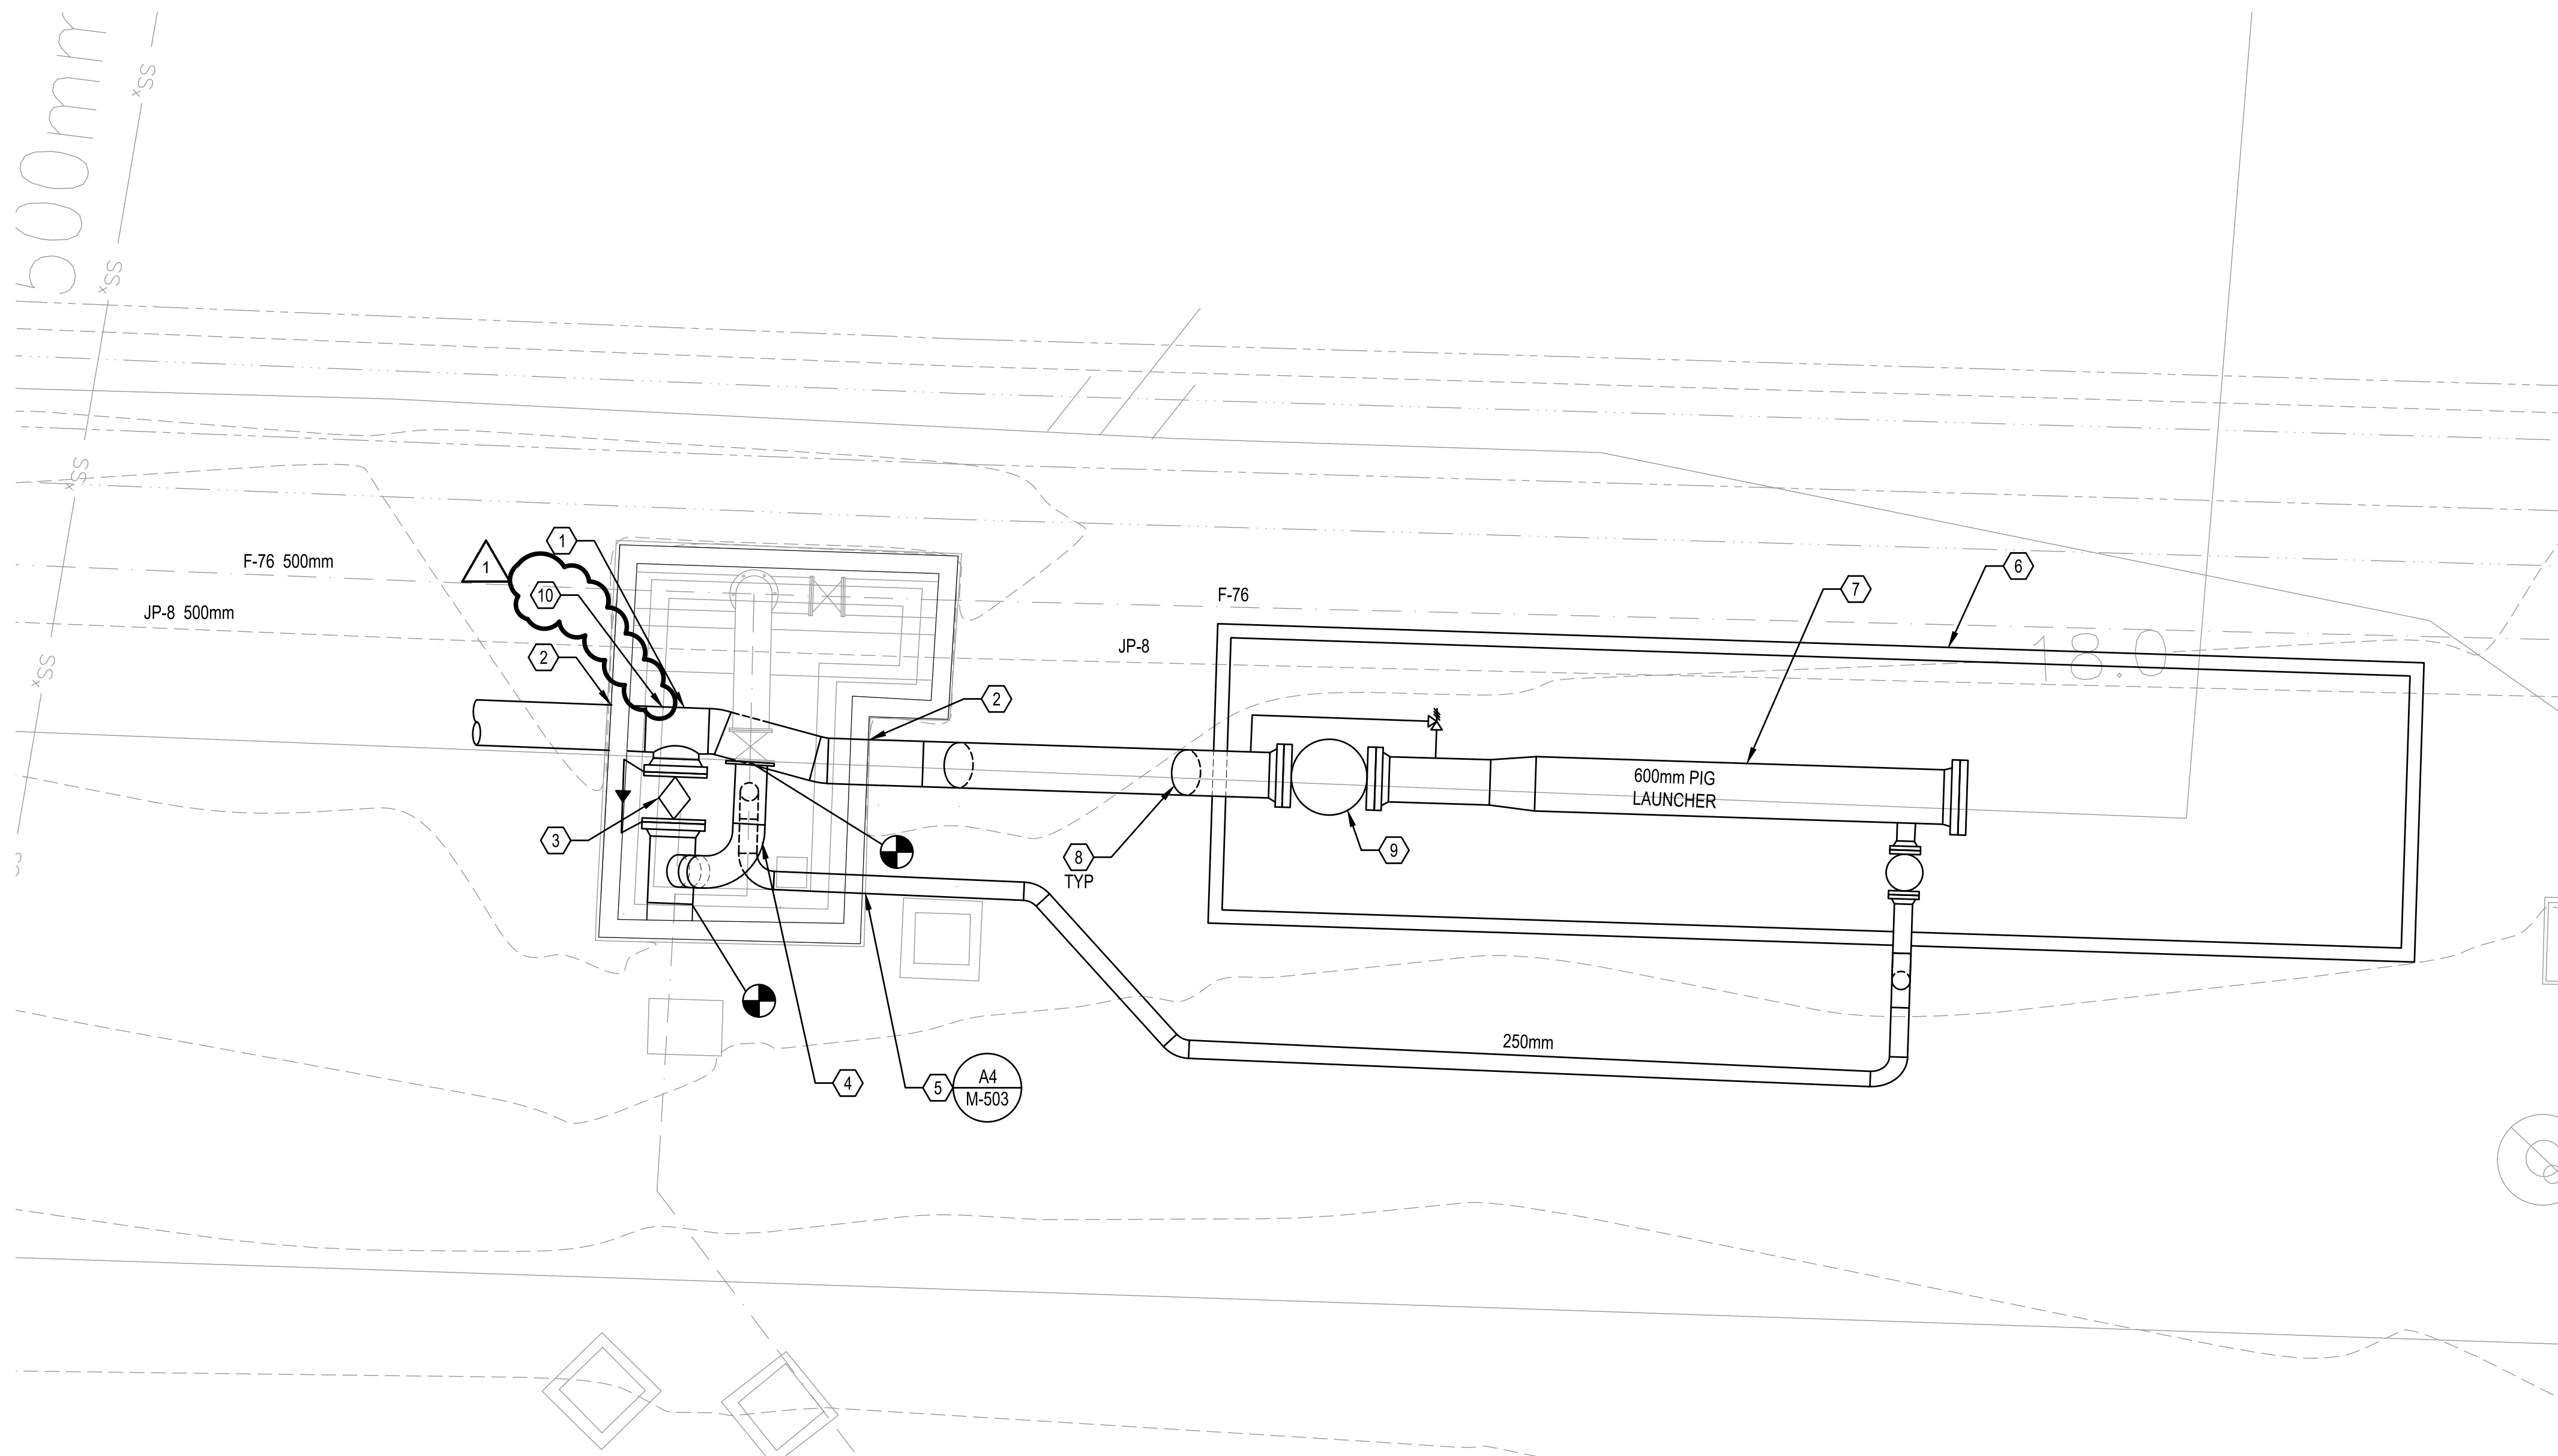

B1 PLAN - ML-2 MANHOLE
PLANTA - POZO ML-2
1:50

KEYED NOTES:
NOTAS DE REFERENCIA:

- PROVIDE 500mm F-76.
PROVEER TUBERÍA F-76 DE 500mm.
- REPAIR VALVE PIT WALL PENETRATION AROUND 500mm PIPE AS NEEDED. REHABILITATE DAMAGED CONCRETE IN ACCORDANCE WITH SPECIFICATION 03 01 00 AND ACI 562-16.
REPARAR LA PENETRACIÓN DE LA PARED DE LA FOSA PARA LA VÁLVULA ALREDEDOR DE LA TUBERÍA DE 500mm SEGÚN SE NECESITE. REPARAR EL HORMIGÓN DAÑADO DE ACUERDO A LA ESPECIFICACIÓN 03 01 00 Y ACI 562-16.
- PROVIDE DBB PLUG VALVE WITH THERMAL RELIEF
PROVEER DE DOBLE BLOQUEO Y DESCARGA CON ALIVIO TÉRMICO.
- 350mm F-76
TUBERÍA F-76 DE 350mm.
- CUT OPENING IN WALL FOR PIPE PENETRATION AND PROVIDE SLEEVE
ABRIR HUECO EN PARED PARA PENETRACIÓN DE TUBERÍA Y PROVEER PASATUBOS
- PROVIDE CURBED CONCRETE CONTAINMENT PAD FOR PIG LAUNCHER.
PROVEER PLATAFORMA DE CONTENCIÓN DE HORMIGÓN ENCINTADA PARA LANZADOR PIG.
- PROVIDE PIG LAUNCHER WITH CURBED CONCRETE CONTAINMENT PAD. PIG LAUNCHER MUST BE DESIGNED TO ACCOMODATE INTELLIGENT PIGS (IU TOOLS) IN ACCORDANCE WITH REQUIRMENTS OF UFC 3-460-01, CHAPTER 9, AND SPECIFICATION SECTION 33 52 40. VENDOR MUST CONFIRM SIZE OF BARREL AND KICKER ATTACHMENT LOCATION.
PROVEER LANZADOR PIG CON PLATAFORMA CONTENEDORA DE HORMIGÓN CON BORDILLO. EL LANZADOR PIF DEBERÁ ESTAR DISEÑADO PARA ACOGER LOS PIG INTELIGENTES (HERRAMIENTAS IU) DE ACUERDO CON LOS REQUERIMIENTOS DE UFC 3-460-01, CAPÍTULO 9, Y ESPICIFICACIÓN SECCIÓN 33 52 40. EL CONTRATISTA DEBERÁ CONFIRMAR EL TAMAÑO DEL TUBO.
- PROVIDE 3 DIAMETER BEND RADIUS ELBOW.
PROVEER UN CODO DE RADIO DE CURVATURA DE 3 DIÁMETRO.
- PROVIDE FULL PORT DB&B BALL VALVE (PIGGABLE) WITH THERMAL RELIEF.
PROVEER LA VÁLVULA DE BOLA DB&B DE PUERTO COMPLETO (PIGGABLE) CON ALIVIO TÉRMICO.
- PROVIDE TEE WITH GUIDE BARS.
PROVEER TE CON BARRAS GUIA.

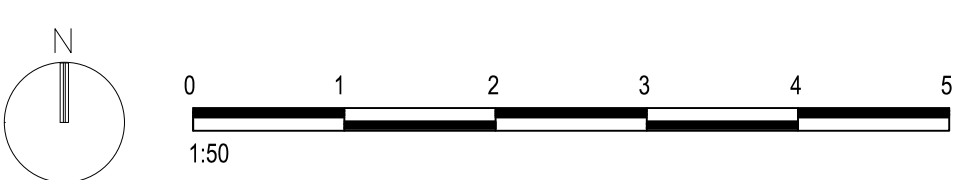

DATE		01-30-2026	TS
SYN		1	ADDED KEY NOTE
DESCRIPTION			

225 Iowa Avenue, Muscatine, Iowa 52761-3764
www.stanleyconsultants.com
A/E INFO

FOR COMMANDER NAVFAC	
ACTIVITY	
SATISFACTORY TO DATE	
DES. TAS	DRAW. GMR CHK. JV
PM/DM CCA/EAL	
BRANCH MANAGER	
DESIGN MANAGER	
FIRE PROTECTION	


DEPARTMENT OF THE NAVY
NAVAL FACILITIES ENGINEERING SYSTEM COMMAND ~ ATLANTIC
ATLANTIC DESIGN AND CONSTRUCTION
NAVAL STATION ROTA
ROTA, SPAIN
WREFOLE, VA

FUEL PIPELINE FROM PIER 3 TO BULK STORAGE
ENLARGED SITE PLAN - ML2
PLANTA EXTERIOR - ML2


SCALE: **AS NOTED**
EPROJECT NO.: **1606884**
CONSTR. CONTR. NO.

NAVFAC DRAWING NO.
14142803

SHEET **102** OF **149**
M-411

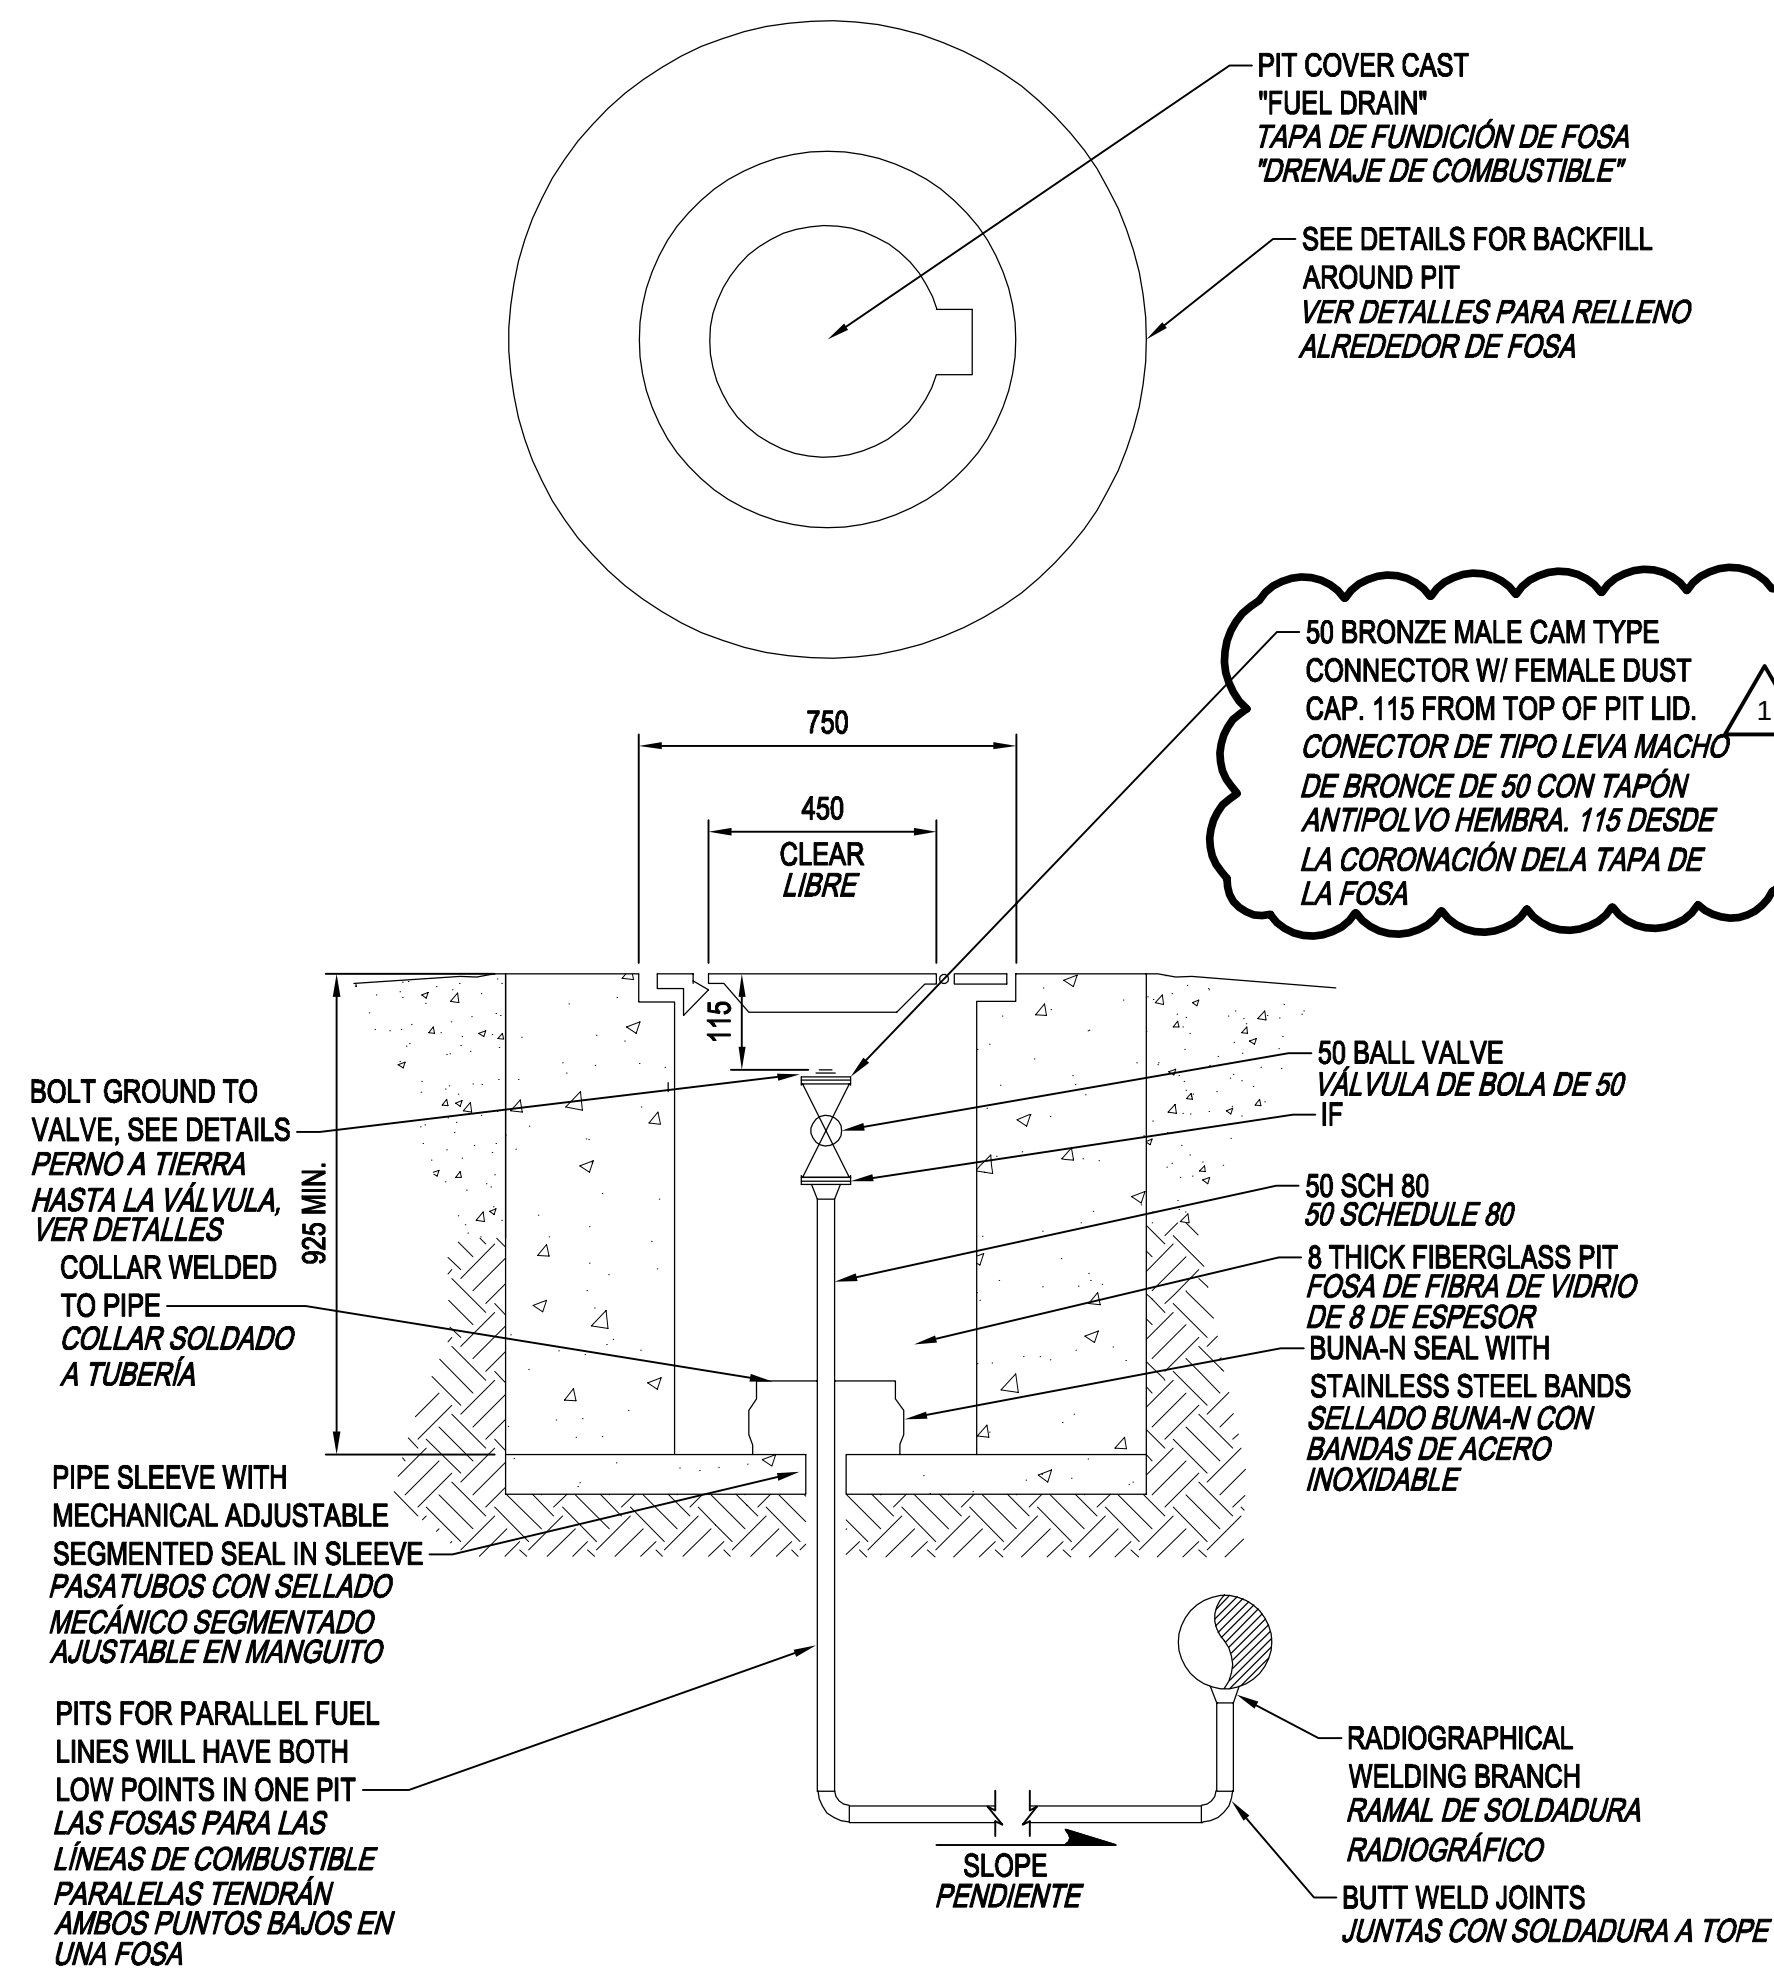


TYPICAL LOW POINT DRAIN PIT
FOSA DE DRENAJE TÍPICA EN PUNTO BAJO

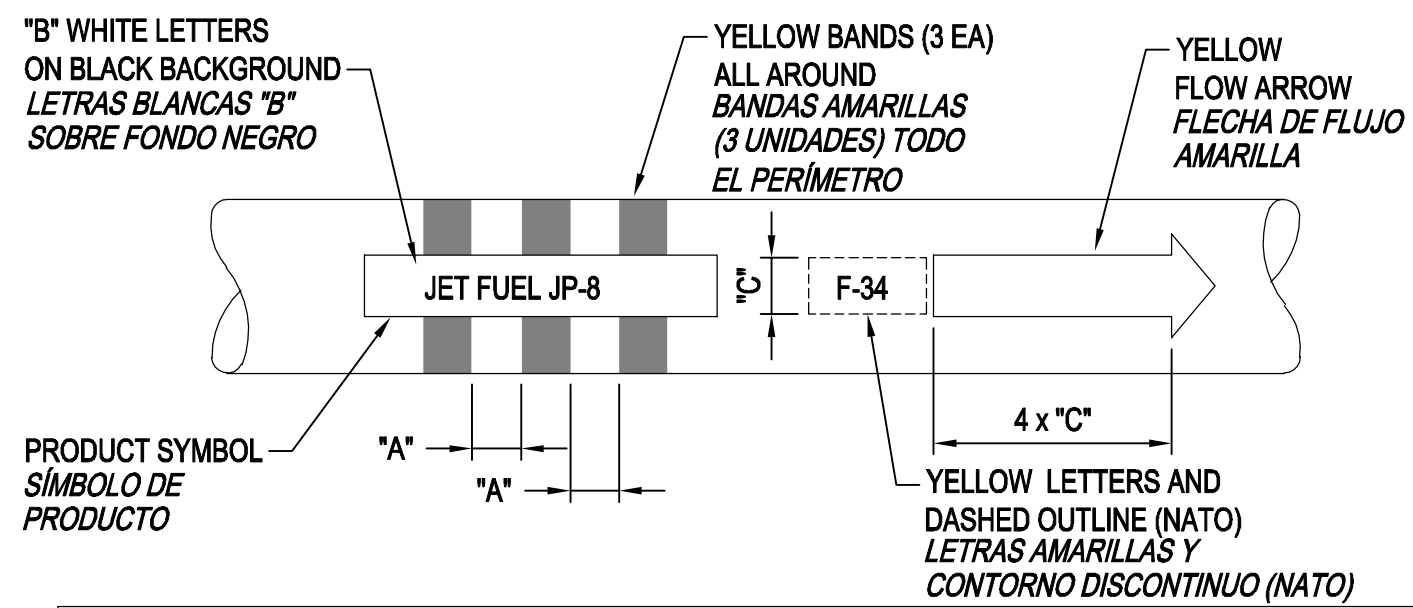


SIZES OF LETTERS AND BANDS TAMAÑOS DE LETRAS Y BANDAS			
PIPE DIAMETER DIÁMETRO DE TUBERÍA (mm)	A BAND WIDTH AND SPACING ANCHO DE BANDA Y ESPACIAMIENTO (mm)	B TITLE LETTER SIZE TAMAÑO LETRA TÍTULO (mm)	C BACKGROUND AND ARROWS FONDO Y FLECHAS (mm)
UNDER 80 / POR DEBAJO DE 80	80	15	25
80-150	80	25	50
150-225	80	50	80
OVER 225 / POR ENCIMA DE 225	100		115


PRODUCT FLOW SYMBOL DETAIL
DETALLE DEL SÍMBOLO DEL FLUJO DEL PRODUCTO

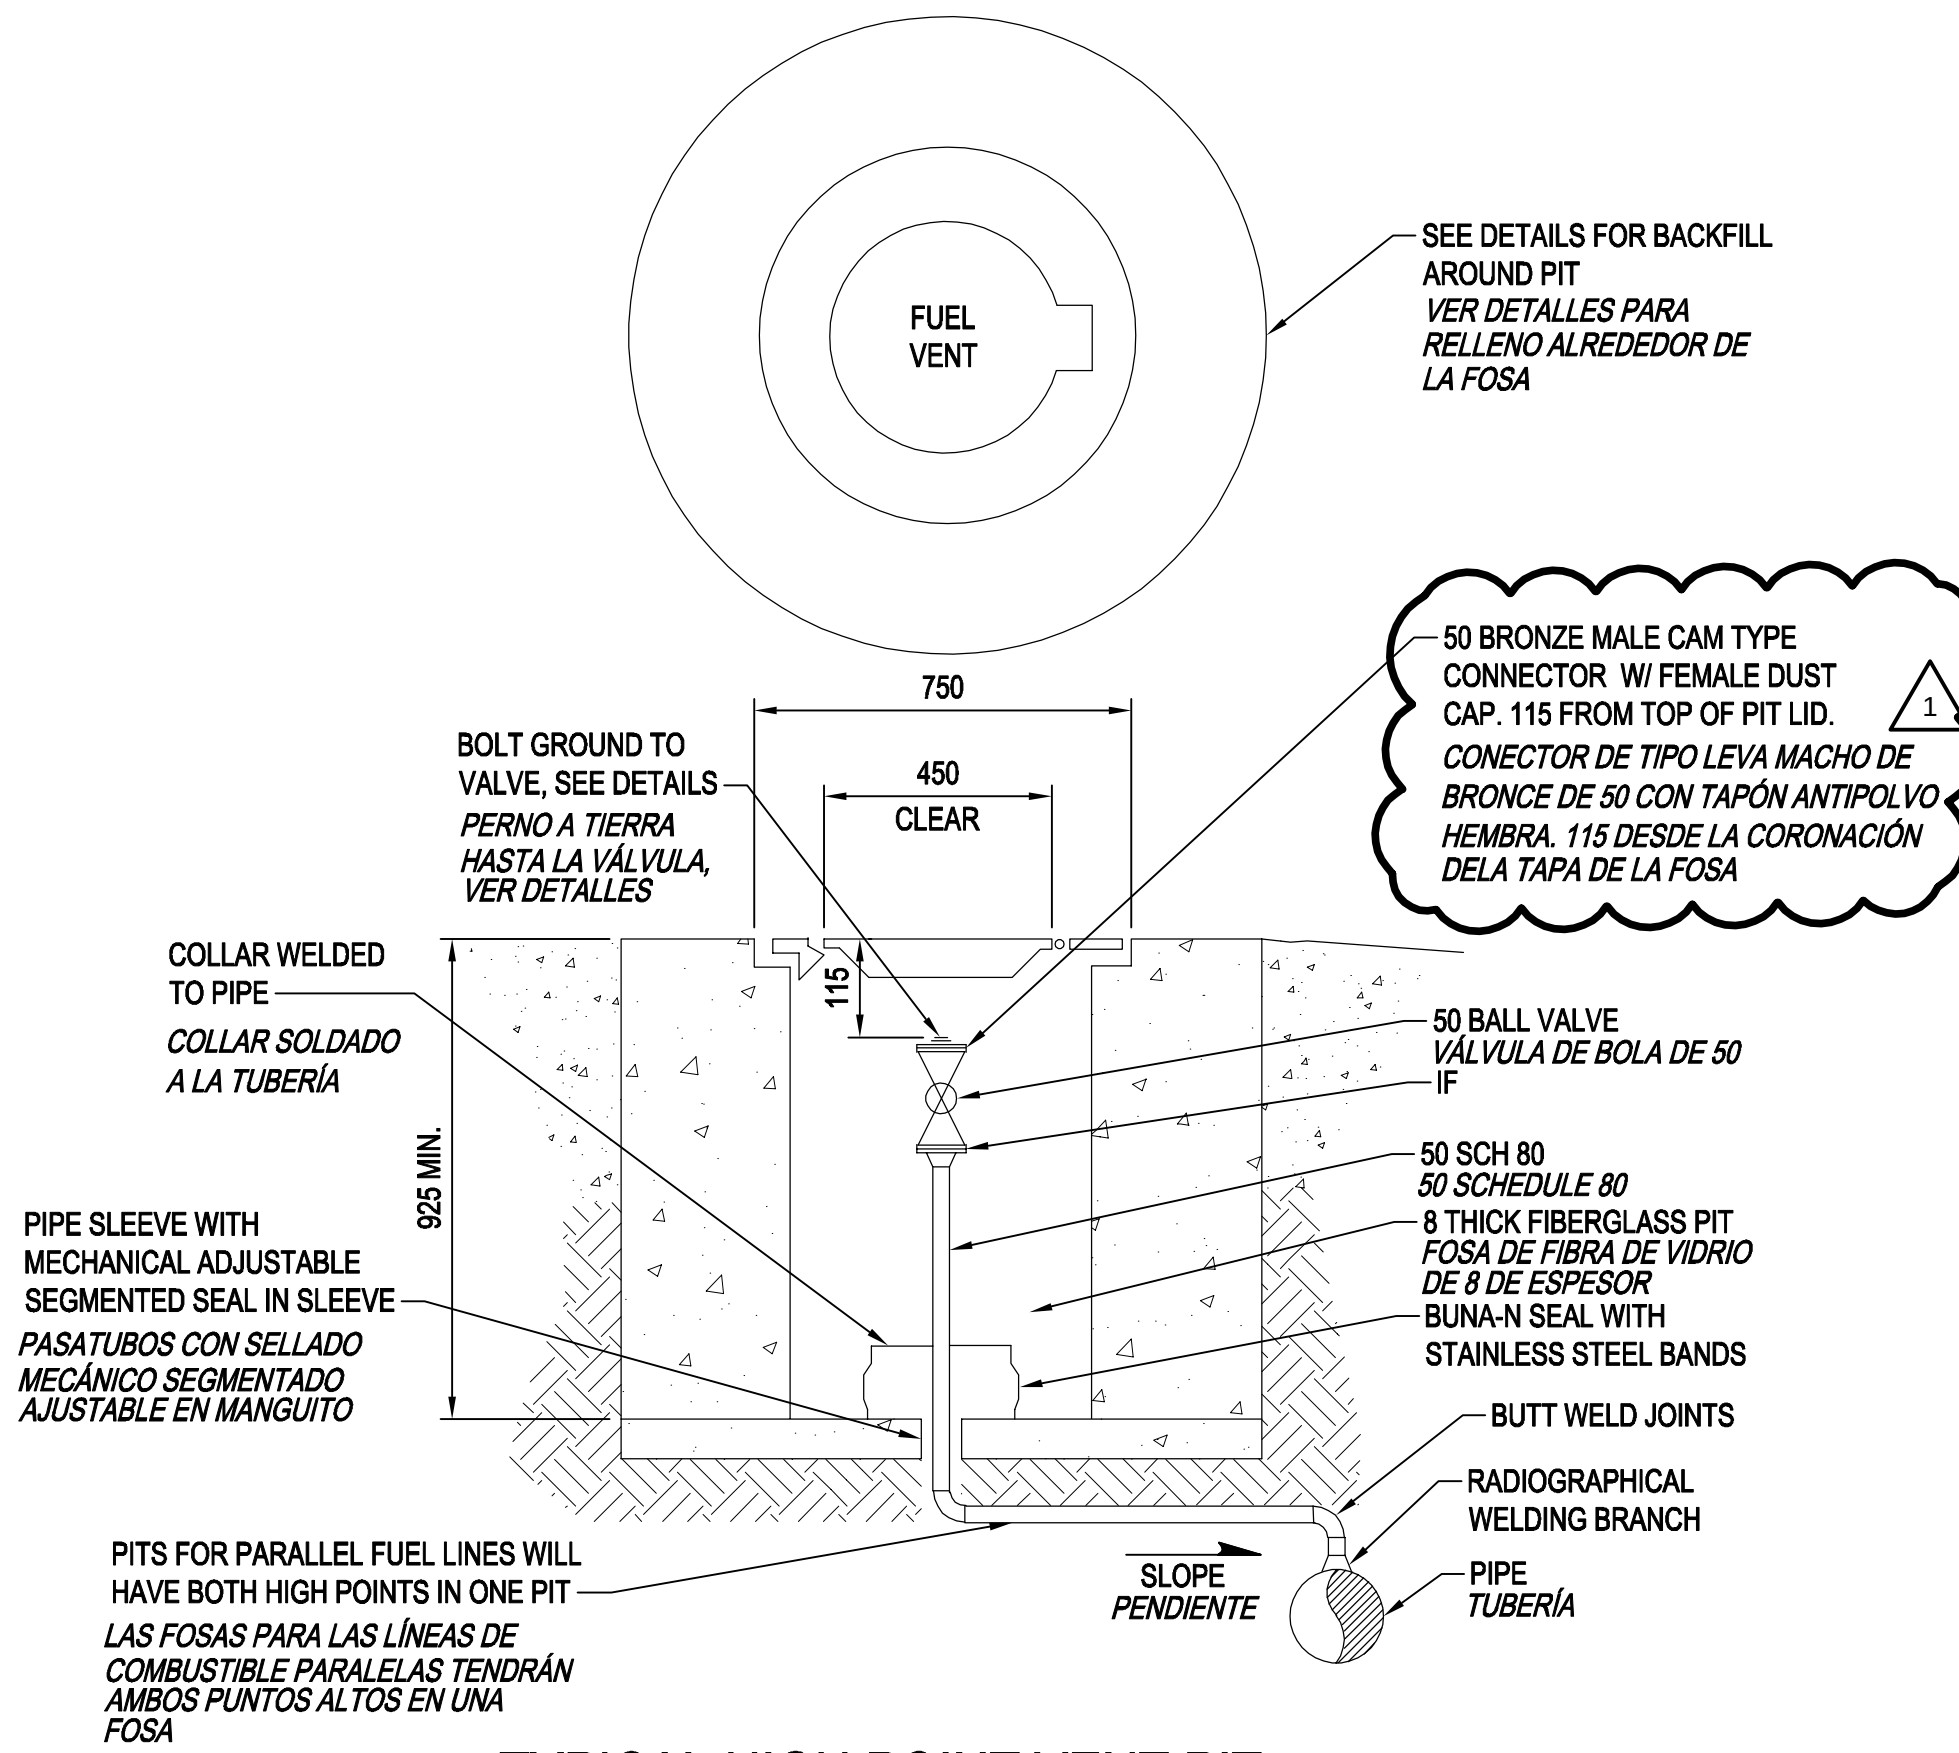

TYPICAL HIGH POINT VENT PIT
FOSA DE VENTEO DE PUNTO ALTO TÍPICA

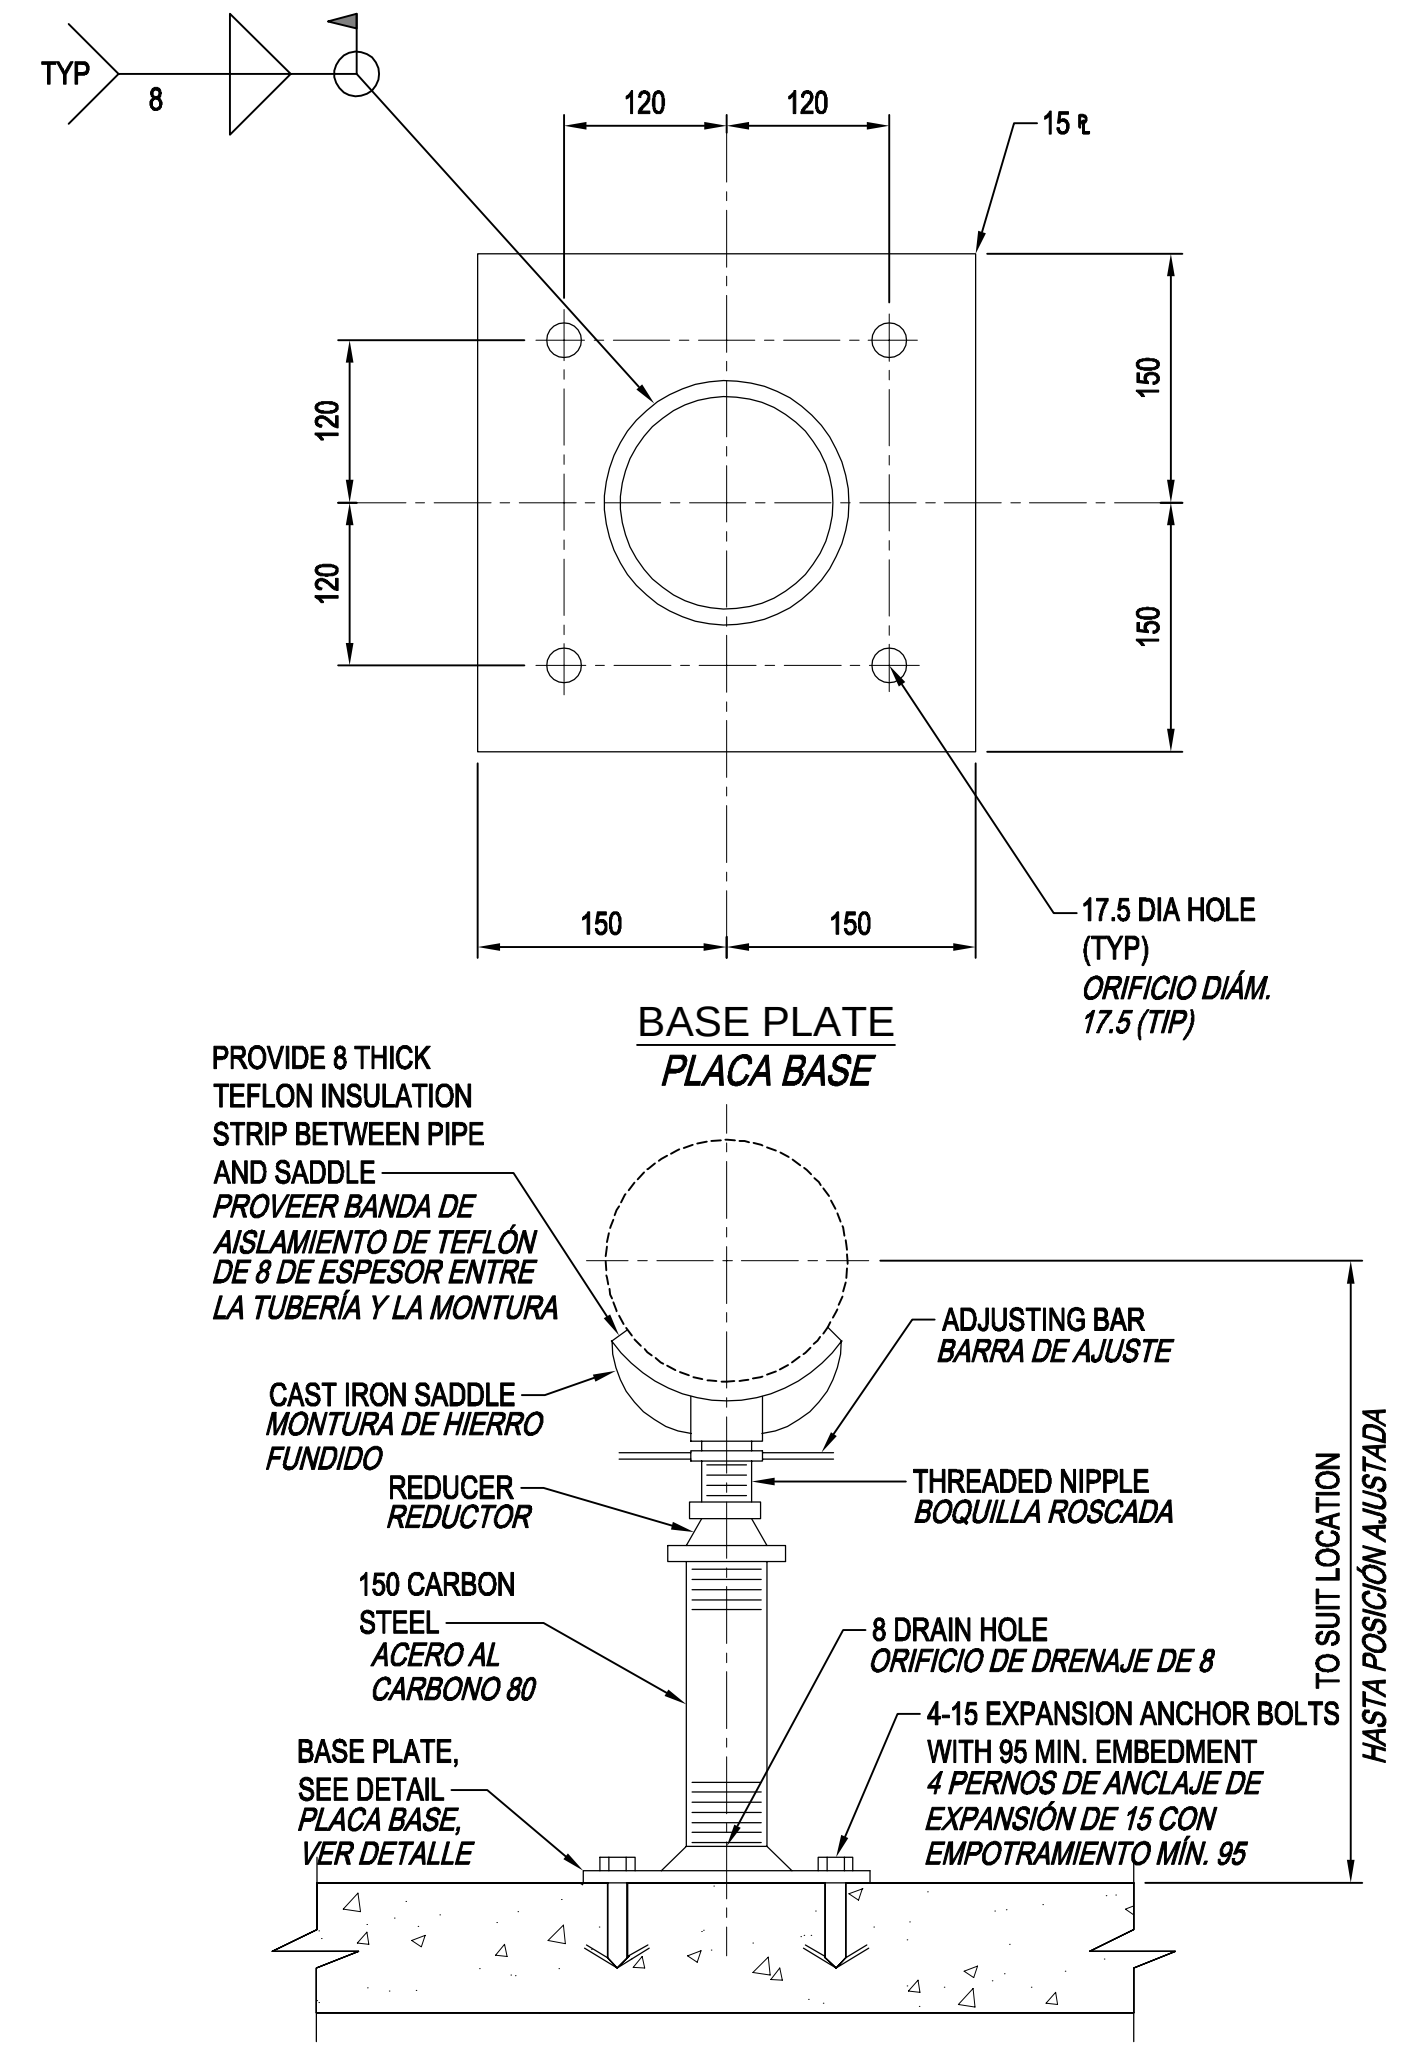

B4 ADJUSTABLE PIPE SADDLE SUPPORT DETAIL
DETALLE DE SOPORTE DE MONTURA AJUSTABLE PARA TUBERÍA
NTS

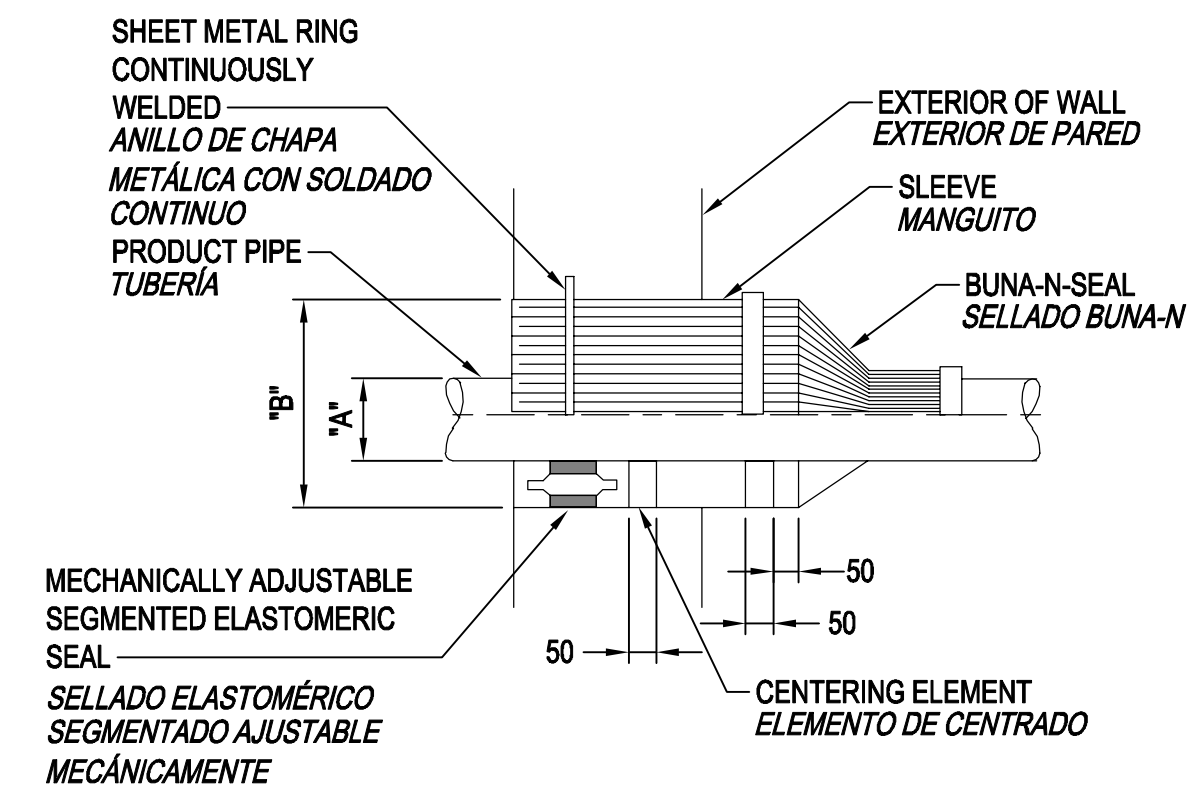

PRODUCT PIPE <i>TUBERIA</i>	A	B
300	310 DIAMETER	400 DIAMETER
200	230 DIAMETER	310 DIAMETER
150	180 DIAMETER	260 DIAMETER
100	115 DIAMETER	230 DIAMETER
50	68 DIAMETER	95 DIAMETER

PIPE PENETRATION DETAIL
DETALLE DE PENETRACIÓN DE TUBERÍA