

FILE NAME: U:\2031423\04-CONV\01-SHEETS\UTL-1606884-C-CD119.dwg LAYOUT NAME: cd119 PLOTTED: Tuesday, January 27, 2026 - 3:34pm USER: 6450




GENERAL NOTES:
NOTAS GENERALES:



- PAVEMENT REMOVAL AND RESTORATION LIMITS FOR UTILITY INSTALLATION ARE APPROXIMATE AND SUBJECT TO CONTRACTOR MEANS AND METHODS.
- LA RETIRADA DEL PAVIMENTO Y LOS LÍMITES DE REPARACIÓN DE DE LAS INSTALACIONES SON APROXIMADOS Y SUJETOS A LOS MEDIOS Y MÉTODOS DEL CONTRATISTA.
- SEE "MD" SHEETS FOR DEMOLITION OF FUEL PIPING.
VER PLANOS "MD" PARA DEMOLICIÓN DE TUBERÍAS DE COMBUSTIBLE.
- SEE "M" SHEETS FOR FUEL PIPING ALIGNMENT INFORMATION.
VER PLANOS "M" PARA ALINEACIÓN DE TUBERÍAS.
- MAINTAIN EROSION AND SEDIMENT CONTROL MEASUREMENTS UNTIL ALL DISTURBANCE ACTIVITIES ARE COMPLETED.
- MANTENER LAS MEDIDAS DE CONTROL DE EROSIÓN Y SEDIMENTOS HASTA QUE FINALICEN TODOS LOS TRABAJOS.
- RECORD ELEVATIONS OF EXISTING PAVEMENTS PRIOR TO REMOVAL.
ANOTAR LAS ELEVACIONES DE LOS PAVIMENTOS EXISTENTES ANTES DE SU RETIRADA.
- COORDINATE ALLOWABLE LANE CLOSURES WITH CONTRACTING OFFICER. ONE LANE OF TRAFFIC MUST BE MAINTAINED AT ALL TIMES FOR USE OF LOCAL TRAFFIC AND EMERGENCY VEHICLES. SUBMIT TRAFFIC AND PEDESTRIAN CONTROL PLANS FOR APPROVAL A MINIMUM OF 45 DAYS PRIOR TO START OF CONSTRUCTION. PEDESTRIAN AND VEHICLE PARKING ACCESS MUST BE MAINTAINED TO BUILDINGS 134 AND 1741 AT ALL TIMES.
- COORDINAR LOS CORTES DE CARRETERA PERMITIDOS CON EL OFICIAL CONTRATANTE. SE DEBE MANTENER UN CARRIL DE CIRCULACIÓN EN TODO MOMENTO PARA EL TRÁFICO LOCAL Y LOS VEHÍCULOS DE EMERGENCIA. PRESENTAR LOS PLANES DE CONTROL DE TRÁFICO DE VEHÍCULOS Y DE PEATONES PARA SU APROBACIÓN CON UN MÍNIMO DE 45 DÍAS ANTES DEL INICIO DE LAS OBRAS. SE DEBERÁ MANTENER EN TODO MOMENTO EL ACCESO DE PEATONES Y VEHÍCULOS A LOS EDIFICIOS 134 Y 1741.

KEYED NOTES:
NOTAS DE REFERENCIA:

- REMOVE CHAIN LINK FENCE
RETIRAR VALLA DE SIMPLE TORSIÓN
- APPROXIMATE TRENCH LIMITS
LÍMITES APROXIMADOS DE ZANJA
- FULL DEPTH SAWCUT
CORTE DE SIERRA DE PROFUNDIDAD COMPLETA
- DO NOT DISTURB ELECTRIC BOX
NO ALTERAR ARQUETA ELÉCTRICA
- PROTECT MANHOLE FOUNDATION IN PLACE
RETIRAR CIMENTACIÓN DE POZO IN SITU
- DO NOT DISTURB POWER POLE
NO ALTERAR POSTE DE FUERZA
- CATHODIC PROTECTION BOND BOX AND TEST STATION. SEE SHEET EC-109
CAJA DE EMPALMES Y ESTACIÓN DE PRUEBAS DEL SISTEMA DE PROTECCIÓN CATÓDICA. VER PLANO EC-109
- MODIFY PENETRATIONS AT EXISTING HIGH-POINT VENT AND LOW-POINT DRAIN PITS TO INSTALL 500mm PIPE. FILL IN EXISTING PENETRATIONS SEE STRUCTURAL DETAILS ON SHEET S-521.
- MODIFICAR PENETRACIONES EN EL PUNTO ALTO DEL VENTEO EXISTENTE Y EN EL PUNTO BAJO LA FOSA DE DRENAJE EXISTENTE PARA INSTALAR TUBERÍA DE 500mm. RELLENAR PENETRACIONES EXISTENTES. VER DETALLES DE ESTRUCTURA EN PLANO S-521.
- SILT FENCE
VALLA DE CIEÑO
- FILTER SOCK
CALCETÍN DE FILTRO

DEMOLITION LEGEND:
LEYENDA DE DEMOLICIÓN:

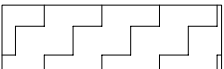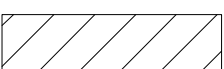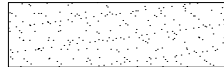- APPROXIMATE TRENCH LIMITS
LÍMITES APROXIMADOS DE ZANJA
-  REMOVE EXISTING PCC. REMOVE TO CLOSEST JOINT LINE
RETIRAR HORMIGÓN EXISTENTE. RETIRAR HASTA LA JUNTA MÁS CERCANA
-  REMOVE EXISTING ASPHALT PAVING
RETIRAR PAVIMENTO DE ASFALTO EXISTENTE
-  REMOVE AGGREGATE
RETIRAR ÁRIDOS
-  REMOVE EXISTING SIDEWALK
RETIRAR ACERADO EXISTENTE
-  REMOVE TREE/SHRUB
RETIRAR ÁRBOL / ARBUSTO

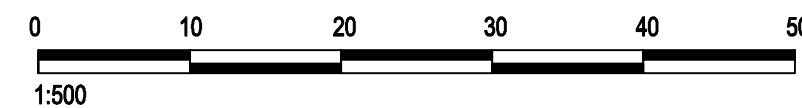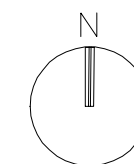


V-BRDG-OTLN



1	REVISED SCALE	01-30-2026	CW	APPR	
1	DESCRIPTION				
					
					
					
APPROVED					
FOR COMMANDER NAVFAC					
ACTIVITY					
SATISFACTORY TO DATE					
DES	CSW	DRW	GMR	CHK	BJF
PM/DM	CCA/EIL				
BRANCH MANAGER					
DESIGN MANAGER					
FIRE PROTECTION					
NAVAL FACILITIES ENGINEERING SYSTEM COMMAND					
NAVAL FACILITIES ENGINEERING SYSTEM COMMAND ~ ATLANTIC					
ATLANTIC DESIGN AND CONSTRUCTION					
NAVAL STATION ROTA					
ROTA, SPAIN					
REPLACE					
FUEL PIPELINE FROM PIER 3 TO BULK STORAGE					
DEMOLITION PLAN					
PLANTA DE DEMOLICIÓN					
SCALE: 1:500					
EPROJECT NO.: 1606884					
CONSTR. CONTR. NO.					
NAVFAC DRAWING NO. 14142722					
SHEET 21 OF 149					
CD119					

FILE NAME: I:\X2931423\04-CON\01-SHEETS\UTIL-1606884-C-CD120.dwg LAYOUT NAME: cd120 PLOTTED: Tuesday, January 27, 2026 - 3:40pm USER: 6450

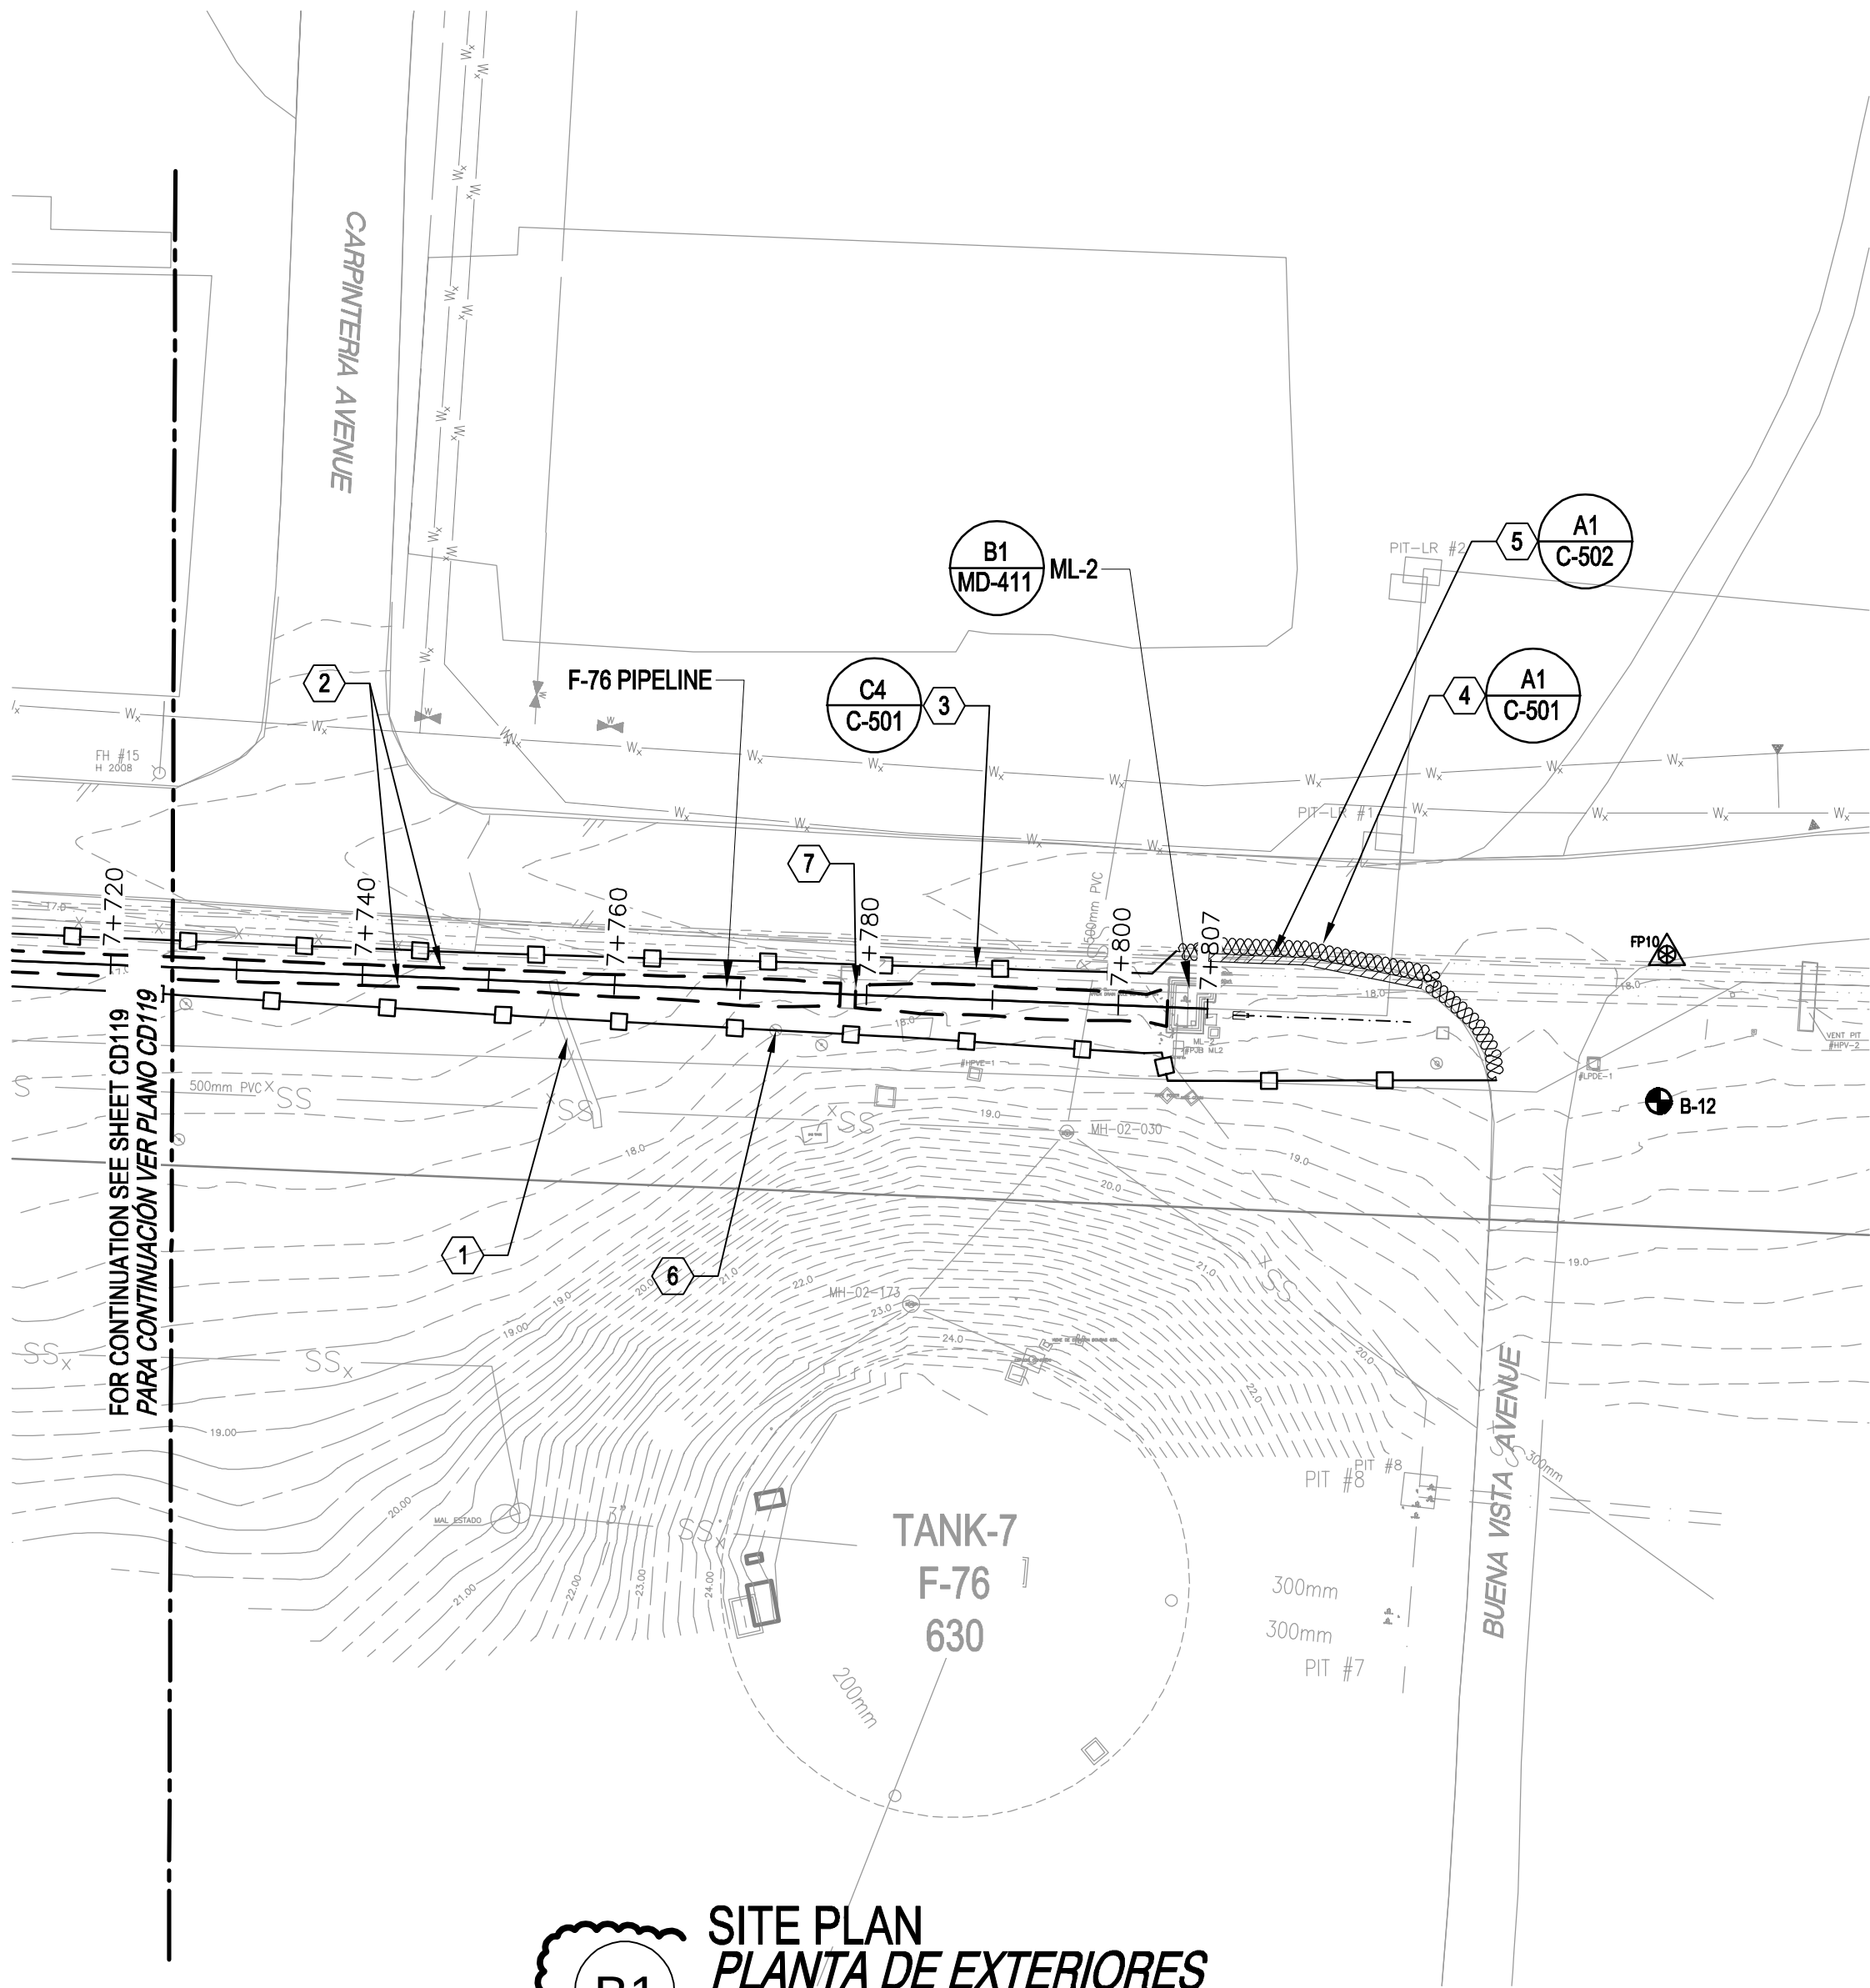

B1 SITE PLAN
PLANTA DE EXTERIORES
1:500

GENERAL NOTES:
NOTAS GENERALES:



- PAVEMENT REMOVAL AND RESTORATION LIMITS FOR UTILITY INSTALLATION ARE APPROXIMATE AND SUBJECT TO CONTRACTOR MEANS AND METHODS.
- LA RETIRADA DEL PAVIMENTO Y LOS LÍMITES DE REPARACIÓN DE DE LAS INSTALACIONES SON APROXIMADOS Y SUJETOS A LOS MEDIOS Y MÉTODOS DEL CONTRATISTA.
- SEE "MD" SHEETS FOR DEMOLITION OF FUEL PIPING.
- VER PLANOS "MD" PARA DEMOLICIÓN DE TUBERÍAS DE COMBUSTIBLE.
- SEE "M" SHEETS FOR FUEL PIPING ALIGNMENT INFORMATION.
- VER PLANOS "M" PARA ALINEACIÓN DE TUBERÍAS.
- MAINTAIN EROSION AND SEDIMENT CONTROL MEASUREMENTS UNTIL ALL DISTURBANCE ACTIVITIES ARE COMPLETED.
- MANTENER LAS MEDIDAS DE CONTROL DE EROSIÓN Y SEDIMENTOS HASTA QUE FINALICEN TODOS LOS TRABAJOS.
- RECORD ELEVATIONS OF EXISTING PAVEMENTS PRIOR TO REMOVAL.
- ANOTAR LAS ELEVACIONES DE LOS PAVIMENTOS EXISTENTES ANTES DE SU RETIRADA.
- COORDINATE ALLOWABLE LANE CLOSURES WITH CONTRACTING OFFICER. ONE LANE OF TRAFFIC MUST BE MAINTAINED AT ALL TIMES FOR USE OF LOCAL TRAFFIC AND EMERGENCY VEHICLES. SUBMIT TRAFFIC AND PEDESTRIAN CONTROL PLANS FOR APPROVAL A MINIMUM OF 45 DAYS PRIOR TO START OF CONSTRUCTION. PEDESTRIAN AND VEHICLE PARKING ACCESS MUST BE MAINTAINED TO BUILDINGS 134 AND 1741 AT ALL TIMES.
- COORDINAR LOS CORTES DE CARRETERA PERMITIDOS CON EL OFICIAL CONTRATANTE. SE DEBE MANTENER UN CARRIL DE CIRCULACIÓN EN TODO MOMENTO PARA EL TRÁFICO LOCAL Y LOS VEHÍCULOS DE EMERGENCIA. PRESENTAR LOS PLANES DE CONTROL DE TRÁFICO DE VEHÍCULOS Y DE PEATONES PARA SU APROBACIÓN CON UN MÍNIMO DE 45 DÍAS ANTES DEL INICIO DE LAS OBRAS. SE DEBERÁ MANTENER EN TODO MOMENTO EL ACCESO DE PEATONES Y VEHÍCULOS A LOS EDIFICIOS 134 Y 1741.

KEYED NOTES:
NOTAS DE REFERENCIA:

- MOVE/REMOVE SURFACE LOG STRUCTURE DURING CONSTRUCTION AND REPLACE UPON COMPLETION
- MOVER / RETIRAR ESTRUCTURA DE SUPERFICIE DURANTE LA CONSTRUCCIÓN Y REINSTALAR TRAS FINALIZAR
- APPROXIMATE TRENCH LIMITS
- LÍMITES APROXIMADOS DE ZANJA
- SILT FENCE
- VALLA DE CIEÑO
- FILTER SOCK
- CALCETÍN DE FILTRO
- MILL ASPHALT FOR KEY-IN SECTION
- FRESAR ASFALTO PARA SECCIÓN EN LLAVE
- DO NOT DISTURB POWER POLE
- NO ALTERAR POSTE DE FUERZA
- MODIFY PENETRATIONS AT EXISTING HIGH-POINT VENT AND LOW-POINT DRAIN PITS TO INSTALL 500mm PIPE. FILL IN EXISTING PENETRATIONS SEE STRUCTURAL DETAILS ON SHEET S-521.
- MODIFICAR PENETRACIONES EN EL PUNTO ALTO DEL VENTEO EXISTENTE Y EN EL PUNTO BAJO LA FOSA DE DRENAJE EXISTENTE PARA INSTALAR TUBERÍA DE 500mm. RELLENAR PENETRACIONES EXISTENTES. VER DETALLES DE ESTRUCTURA EN PLANO S-521.

DEMOLITION LEGEND:
LEYENDA DE DEMOLICIÓN:

- APPROXIMATE TRENCH LIMITS
LÍMITES APROXIMADOS DE ZANJA
- REMOVE EXISTING PCC. REMOVE TO CLOSEST JOINT LINE
RETIRAR HORMIGÓN EXISTENTE. RETIRAR HASTA LA JUNTA MÁS CERCANA
- REMOVE EXISTING ASPHALT PAVING
RETIRAR PAVIMENTO DE ASFALTO EXISTENTE
- REMOVE AGGREGATE
RETIRAR ÁRIDOS
- REMOVE EXISTING SIDEWALK
RETIRAR ACERADO EXISTENTE
- REMOVE TREE/SHRUB
RETIRAR ÁRBOL / ARBUSTO

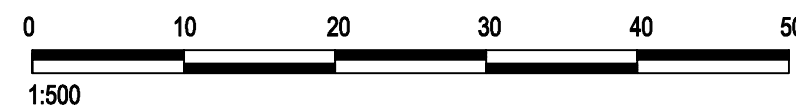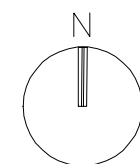

NAVAFAC		Catherine S. Weikel 13864		Stanley Consultants inc. 225 Iowa Avenue, Muscatine, Iowa 52761-3764 www.stanleyconsultants.com		APPROVED FOR COMMANDER NAVAFAC ACTIVITY SATISFACTORY TO: DATE DES: CSW DRW: GMR CHK: BJF PM/DM: CCA/EIL BRANCH MANAGER DESIGN MANAGER FIRE PROTECTION		NAVAFAC ENGINEERING SYSTEM COMMAND NAVAL FACILITIES ENGINEERING SYSTEM COMMAND ~ ATLANTIC ATLANTIC DESIGN AND CONSTRUCTION NAVAL STATION ROTA, SPAIN REPLACE FUEL PIPELINE FROM PIER 3 TO BULK STORAGE DEMOLITION PLAN PLANTA DE DEMOLICIÓN		SCALE: 1:500 EPROJECT NO.: 1606884 CONSTR. CONTR. NO. NAVAFAC DRAWING NO.: 14142723 SHEET 22 OF 149 CD120		REVISED SCALE 1 SYN DESCRIPTION DATE 01-30-2026 CW APPR	
---------	--	------------------------------	--	---	--	---	--	--	--	--	--	--	--

