


FILE NAME: Y:\OCONUS\MultipleSites\2024_1783264_P1360_JAMFAB_Design\DWG\Sheet\13_ELEC\PT1360_1783264_TY501.dwg LAYOUT NAME: TY501 - Electronic Security System Door Elevations PLOTTED: Tuesday, January 20, 2026 - 12:18pm USER: encherian


C1 DOUBLE DOOR ELEVATION FOR ESS ROUGH-IN
SCALE: NOT TO SCALE

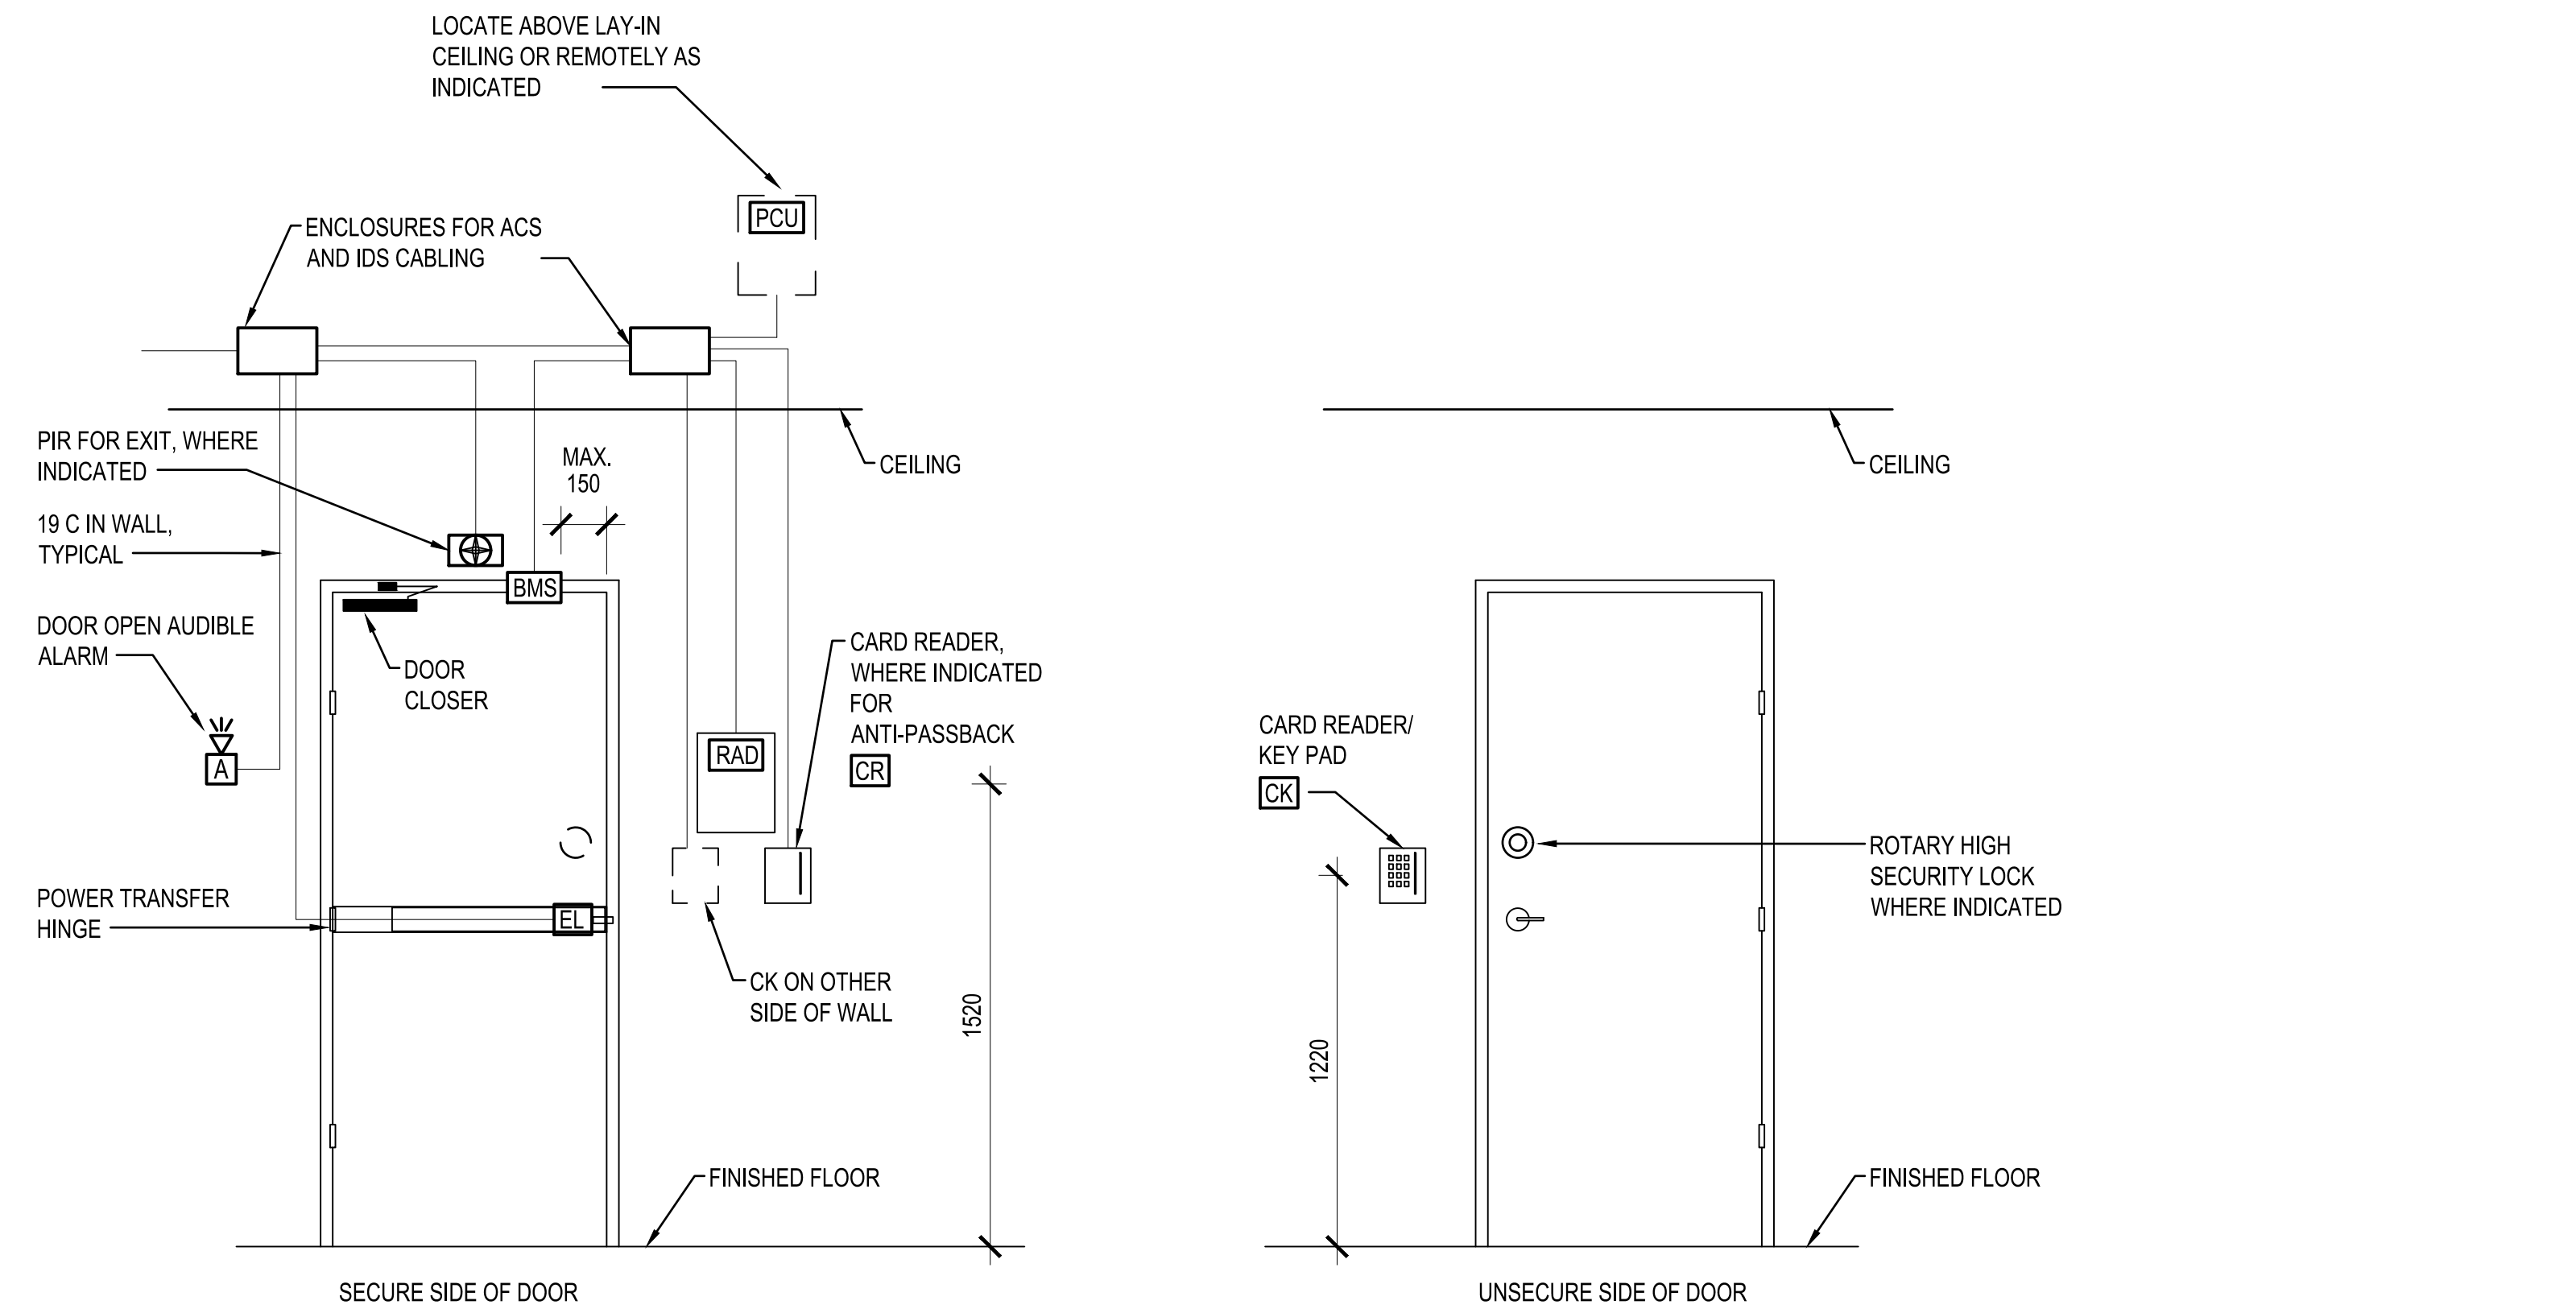

ELEVATION DETAIL NOTES

- ELEVATION DETAILS SHOWN ARE TYPICAL. PROVIDE ROUGH-IN ONLY FOR DEVICES SHOWN ON FLOOR PLAN AND RISER DIAGRAMS.
- COORDINATE WITH DOOR HARDWARE REQUIREMENTS ON SHEET A-606 AND INCLUDED IN PARAGRAPH "HARDWARE SETS" OF SPECIFICATION SECTION 08 71 00 "DOOR HARDWARE".

A1 SINGLE DOOR ELEVATION FOR ESS ROUGH-IN
SCALE: NOT TO SCALE

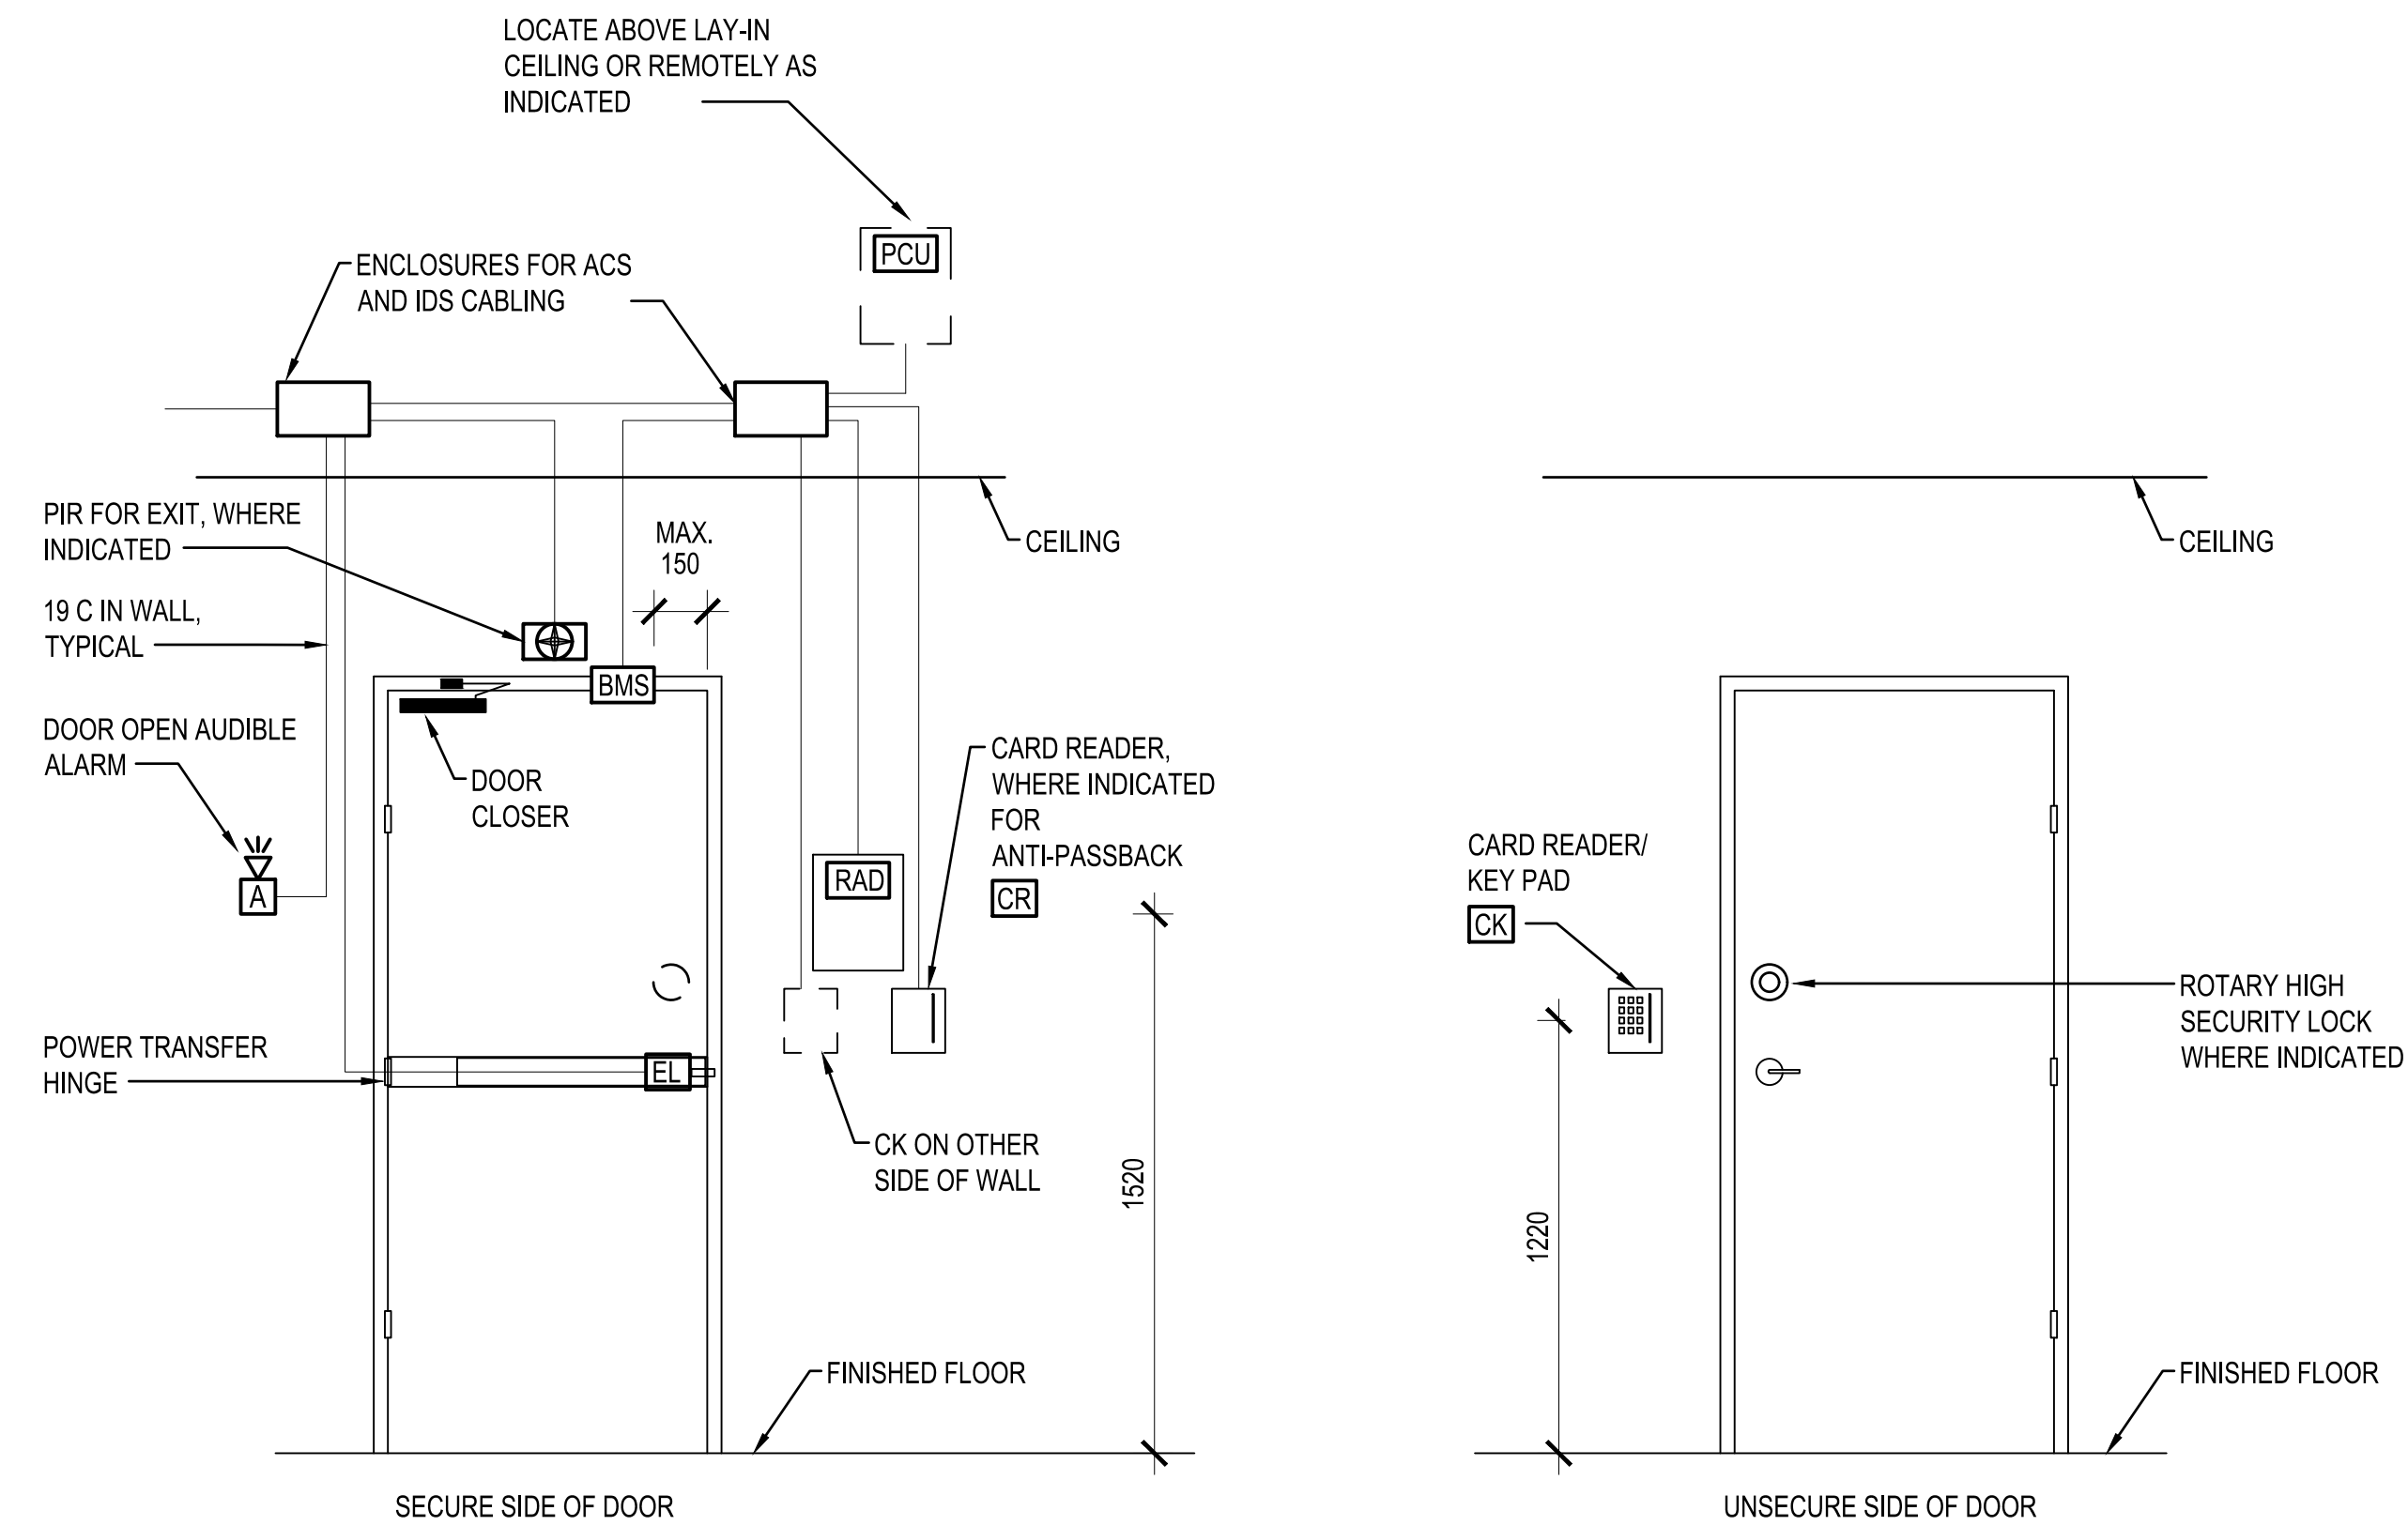

APPROVED

FOR COMMANDER NAVFAC

ACTIVITY

D. EVANS VIA EMAIL

SATISFACTORY TO DATE 01/15/2026

DES CAB DRW CAB CHK SEK

PM/DM MJD/ATP

BRANCH MANAGER SEK

DES PROD DIR WBF

FIRE PROTECTION ENGINEER DSN

DEPARTMENT OF THE NAVY
NAVAL FACILITIES ENGINEERING SYSTEMS COMMAND
PLANNING, DESIGN AND CONSTRUCTION
VARIOUS LOCATIONS

NAVAL FACILITIES ENGINEERING SYSTEMS COMMAND - ATLANTIC
NORFOLK, VA
VARIOUS LOCATIONS

JOINT MARITIME FACILITY

ELECTRONIC SECURITY SYSTEM DOOR ELEVATIONS

SCALE: NONE




APPROVED NO. 1838720

CONSTR. CONTR. NO.

NAVFAC DRAWING NO. 14157230

SHEET 168 OF 170

TY501

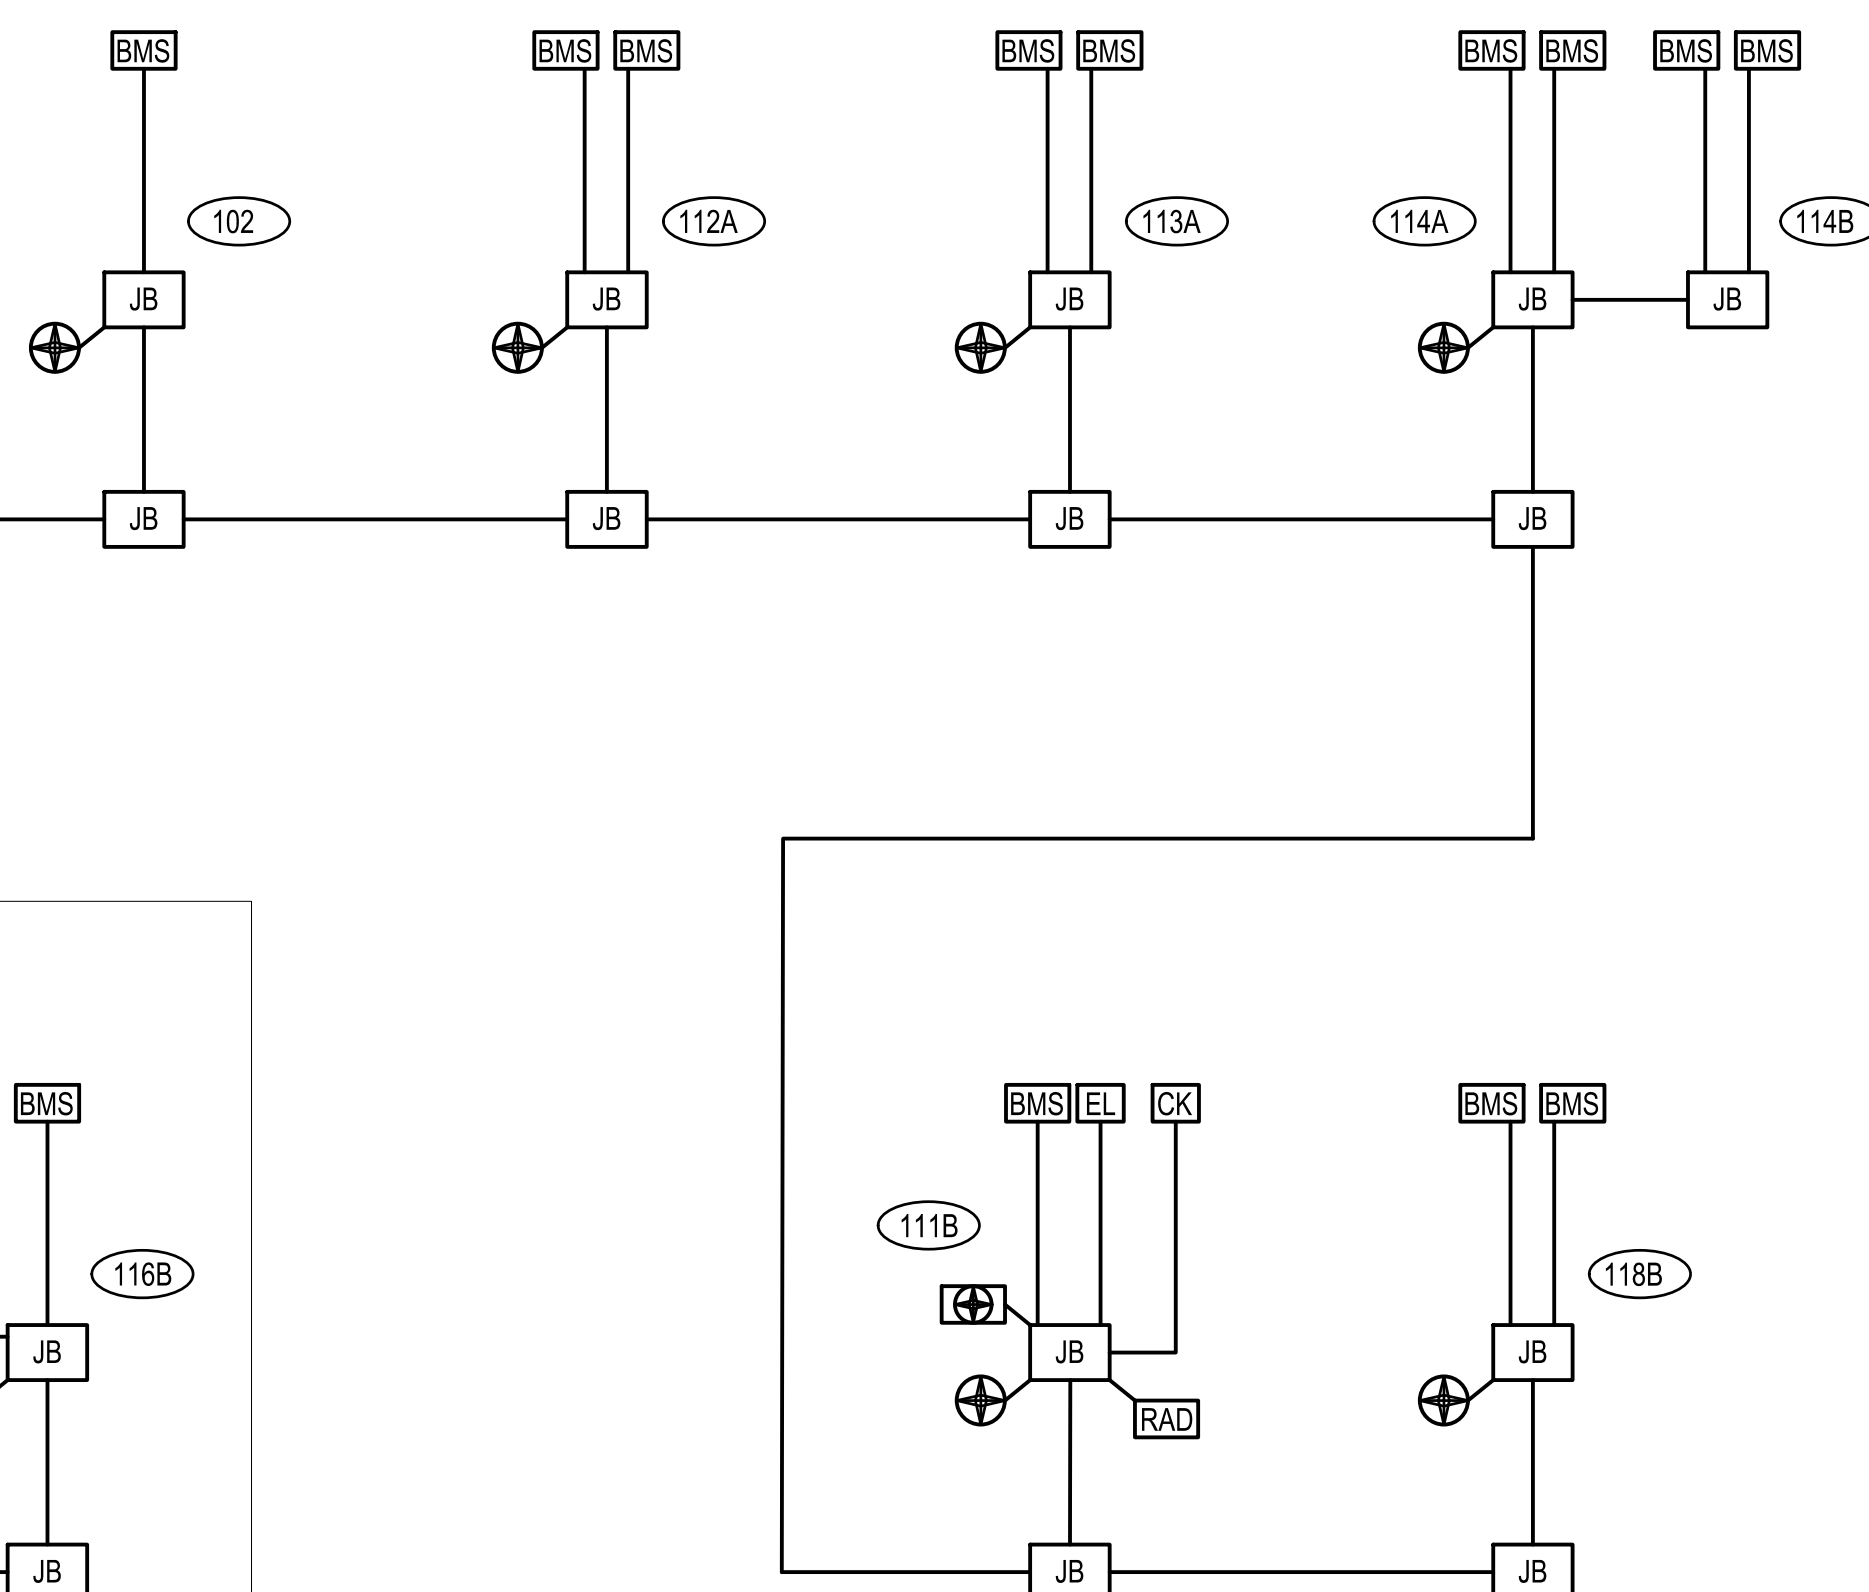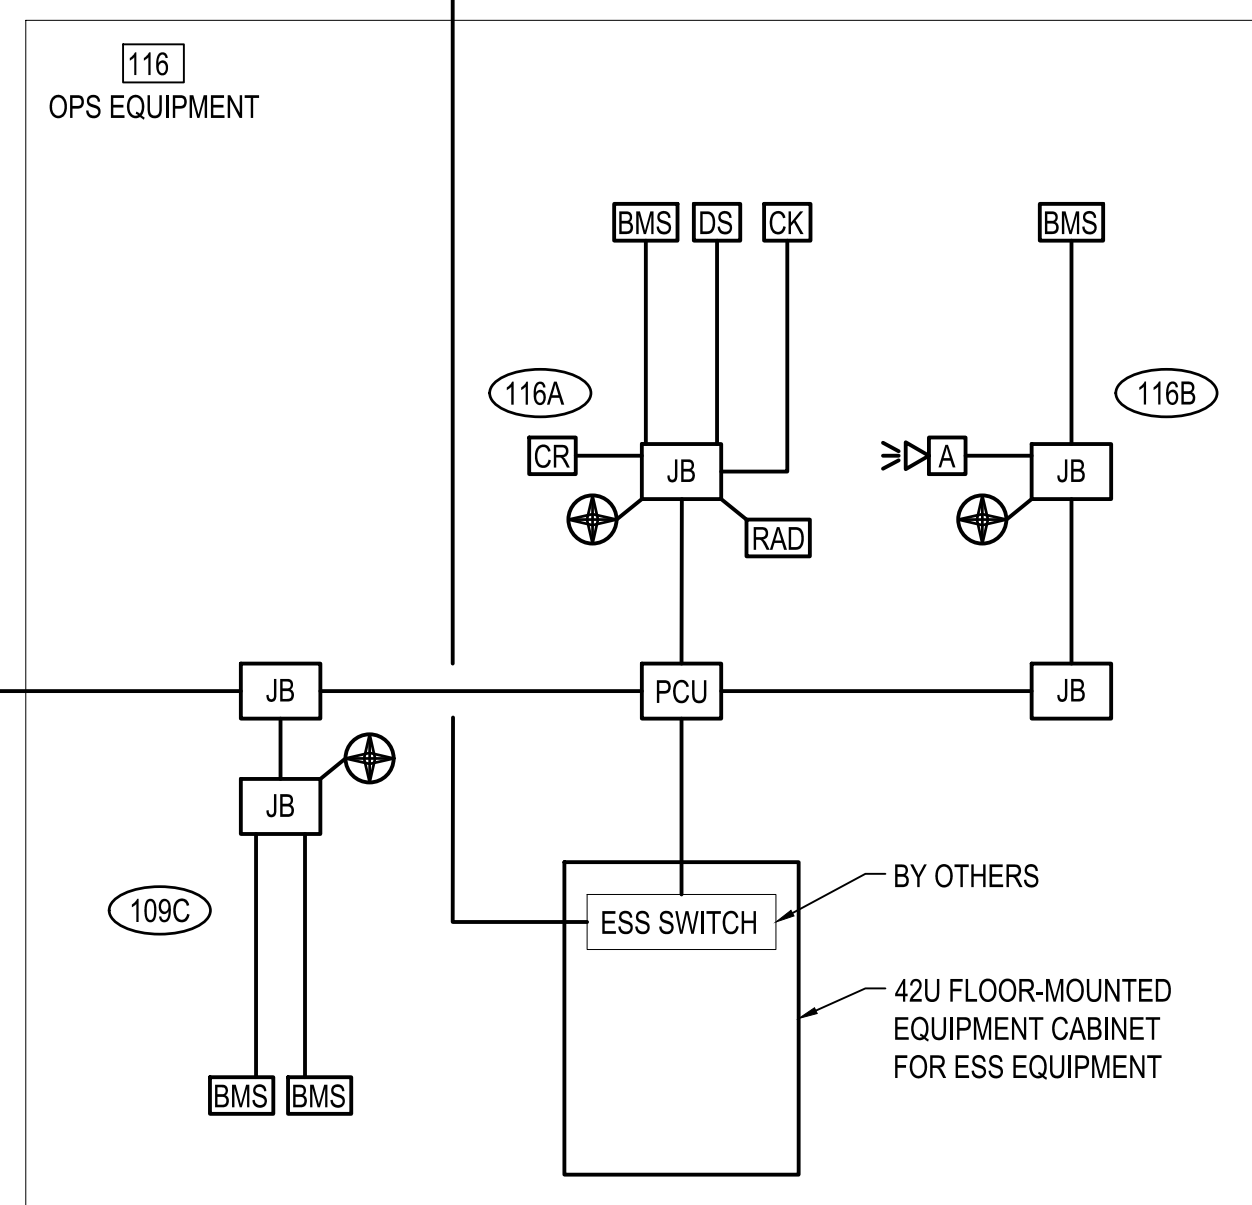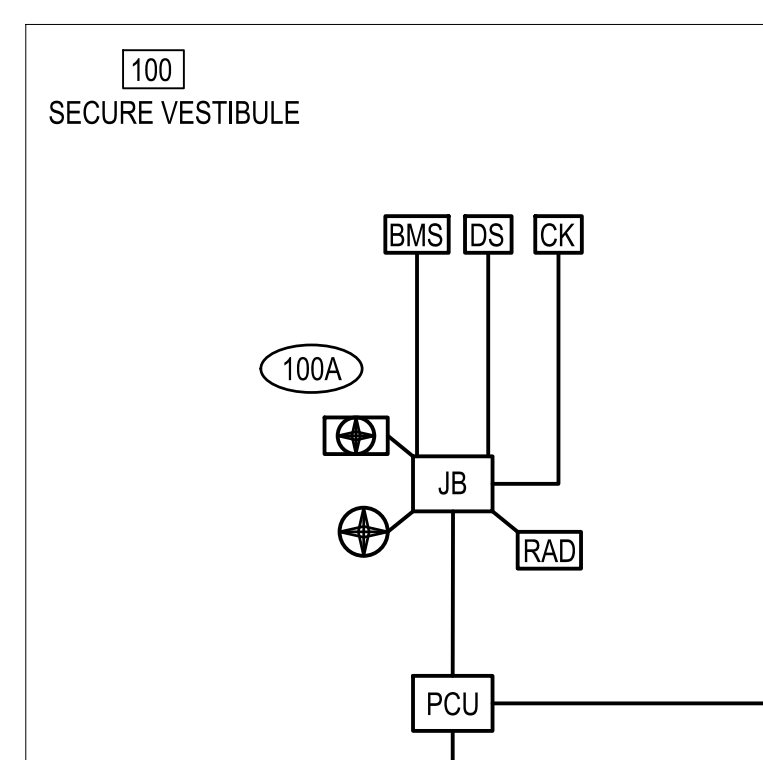


1. PROVIDE GASKETED, WEATHERPROOF BOXES AND COVER PLATES FOR EXTERIOR-MOUNTED DEVICES.
2. PROVIDE DEDICATED WORKSTATION AND MONITOR FOR ESS ENROLLMENT.
3. PROVIDE INFRASTRUCTURE ONLY (CONDUIT, RACEWAYS AND JUNCTION BOXES) FOR ACS AND IDS SYSTEMS DEVICES AND EQUIPMENT. ALL DEVICES, EQUIPMENT, CABLING, INTERCONNECTIONS AND PROGRAMMING BY OTHERS. UON.

- 110 DOOR DESIGNATION
- 162 ROOM DESIGNATION

A1

FILE NAME: Y:\OCONUS\Multiplatform\2024_1783264_P1360_MAMF\B_Design\DWG\Sheet\01_GEN\1360-1783264-G-008.dwg LAYOUT NAME: G-008 PLOTTED: Thursday, November 20, 2025 - 10:08am USER: rodnejbentley

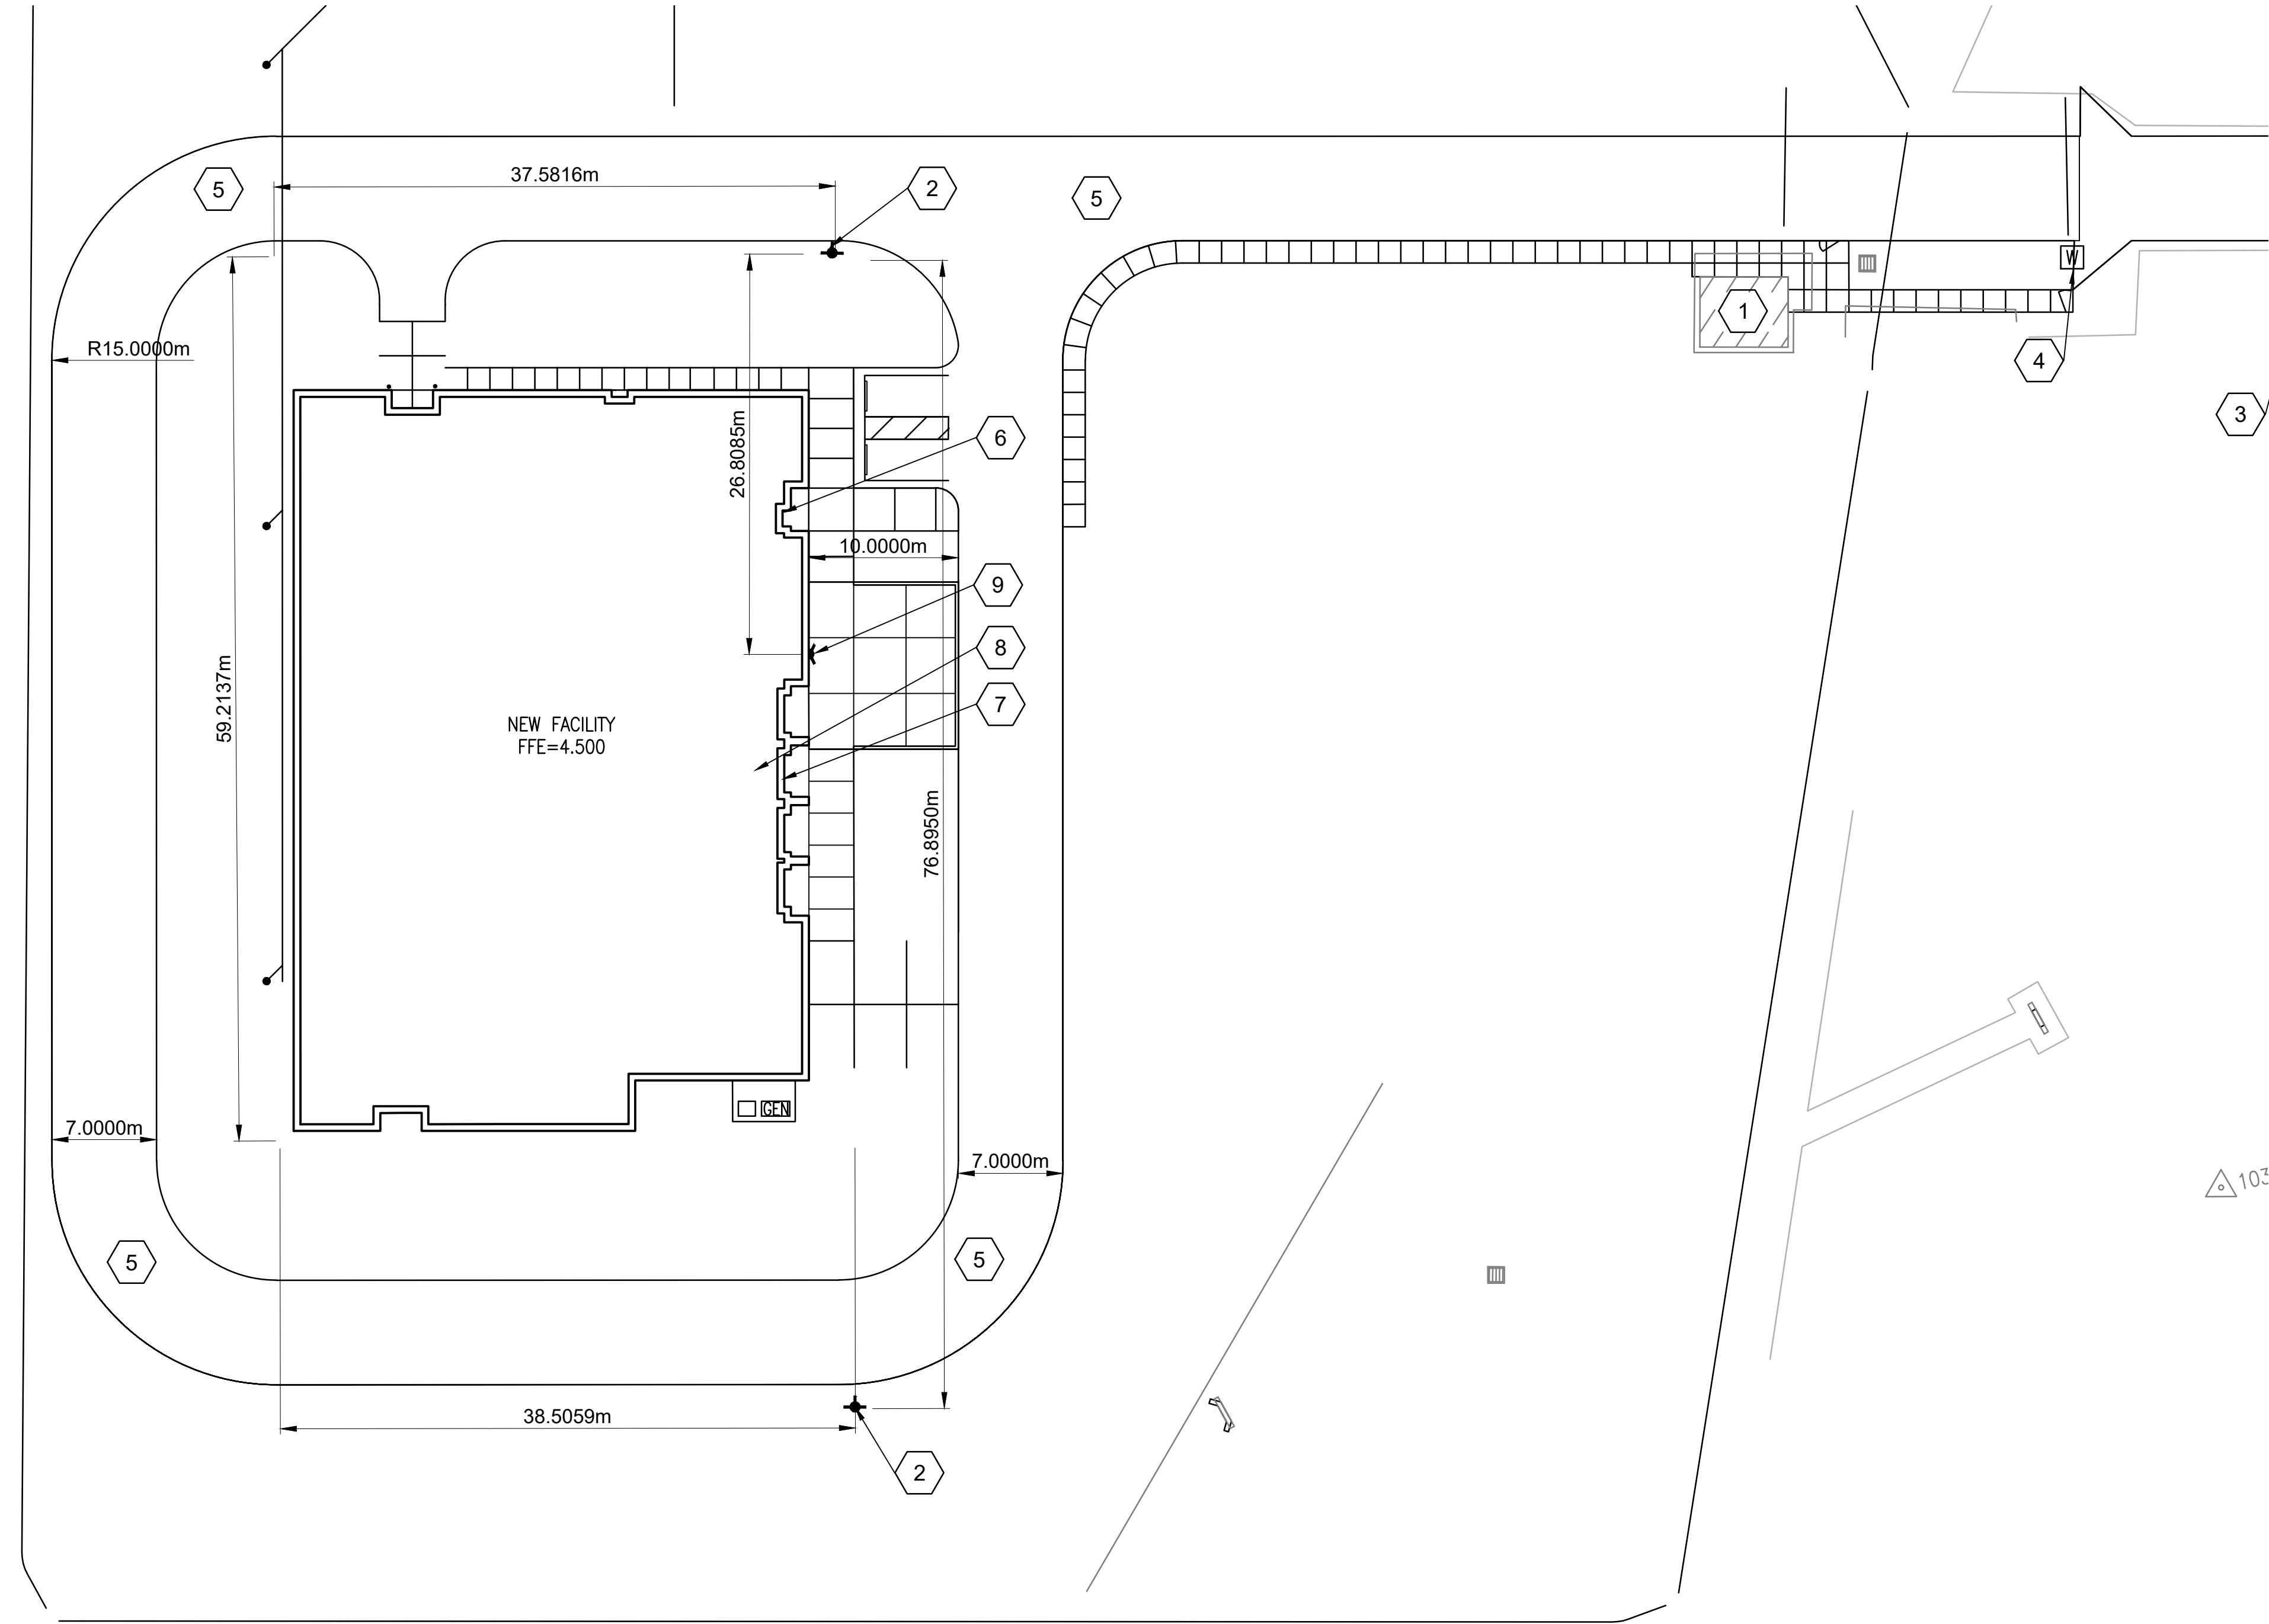

SITE PLAN
SCALE 1:300

GENERAL SHEET NOTES

1. THE EXISTING GUARD SHACK IS MORE THAN 18.3 METERS AWAY FROM THE PROPOSED BUILDING, DEMONSTRATING IT WILL NOT IMPOSE UPON THE PROPERTY LINE OF THE NEW BUILDING.
2. REFER TO CIVIL DRAWINGS FOR MORE INFORMATION.
3. FIRE FLOW FOR THE FACILITY PROVIDES 3550 L/MIN (938 GPM) @ 20PSI. DFPE APPROVED THE REDUCTION IN FIRE FLOW.

SHEET KEYNOTES

- ① EXISTING GUARD BUILDING
- ② NEW FIRE HYDRANT
- ③ EXISTING FIRE HYDRANT
- ④ EMERGENCY KEY BOX LOCATION. REFER TO CIVIL SHEET CU101.
- ⑤ FIRE DEPARTMENT VEHICLE ACCESS IN ACCORDANCE WITH UFC 3-600-01 SECTION 9-1.1
- ⑥ FIRE DEPARTMENT MAIN ENTRY
- ⑦ INCOMING FIRE WATER SERVICE
- ⑧ FIRE PUMP ROOM
- ⑨ FIRE DEPARTMENT CONNECTION



PRELIMINARY
NOT FOR CONSTRUCTION

APPROVED	A/E INFO
FOR COMMANDER NAVFAC	
ACTIVITY	XXXXXX
SATISFACTORY TO	DATE MM/DD/YY
DES RDB	DRW RDB
PM/DM	CHK MAM
BRANCH MANAGER	MJD/ATP
DES PROD DIR	DSN
FIRE PROTECTION ENGINEER	WBF
	DSN

DEPARTMENT OF THE NAVY
NAVAL FACILITIES ENGINEERING SYSTEMS COMMAND
NAVAL FACILITIES ENGINEERING SYSTEMS COMMAND - ATLANTIC
PLANNING, DESIGN AND CONSTRUCTION
NORFOLK, VA
VARIOUS LOCATIONS
VARIOUS LOCATIONS
JOINT MARITIME FACILITY
BUILDING CODE SITE PLAN

GRAPHIC SCALE



SCALE:	AS NOTED
PROJECT NO.:	1838720
CONSTR. CONTR. NO.	#####
NAVFAC DRAWING NO.	#####
SHEET	8 OF ##
G-008	

