

FILE NAME: Y:\OCONUS\MultipleSites\2024_1783264_P1362_JAMFAB_Design\DWG\Sheet\08_ARCH\PT1360_1783264_A106.dwg LAYOUT NAME: A-106 REFLECTED CEILING PLAN PLOTTED: Wednesday, January 21, 2026 - 8:30am USER: paula.lellier1

A1 REFLECTED CEILING PLAN
SCALE: 1:100



GENERAL SHEET NOTES

- A. REFER TO SHEET A-001 FOR ARCHITECTURAL LEGEND AND ABBREVIATIONS.
- C. REFER TO SHEET A-101 FOR KEYNOTES THIS SHEET.
- D. REFER TO SHEET A-605 FOR PARTITION SCHEDULE.
- E. REFER TO SHEET A-606 FOR LOUVER SCHEDULE
- F. SEE INTERIOR 'I' SERIES SHEETS FOR FINISH, FURNITURE AND EQUIPMENT LAYOUTS
- G. PROVIDE FIRE RETARDANT TREATED WOOD BLOCKING FOR MOUNTING OF GRAB BARS, WALL MOUNTED CABINETS, AV OR IT EQUIPMENT, AND WHERE NECESSARY FOR PROPER ATTACHMENT OF ITEMS. SECURELY ATTACH BLOCKING TO METAL STUD FLANGES. COORDINATE EXACT LOCATION AND QUANTITY OF BLOCKING WITH EQUIPMENT REQUIRING REINFORCEMENT.
- H. PROVIDE PLYWOOD BACKBOARDS WHERE REQUIRED FOR COMMUNICATIONS EQUIPMENT. ALL EXPOSED EDGES OF BACKBOARD SHALL BE PAINTED ON FIVE SIDES WITH A FIRE RETARDANT PAINT. SEE ELECTRICAL/TELECOM DRAWINGS FOR ADDITIONAL INFORMATION
- I. FINISH FLOOR ELEVATION IS 0.00mm UNLESS OTHERWISE NOTED.

REFLECTED CEILING PLAN LEGEND

- 150mm x 1200mm LIGHT FIXTURE – SEE ELECTRICAL DRAWINGS
- 150mm x 600mm LIGHT FIXTURE – SEE ELECTRICAL DRAWINGS
- RECESSED CAN LIGHT – SEE ELECTRICAL DRAWINGS
- WALL MOUNTED EXTERIOR LIGHT – SEE ELECTRICAL DRAWINGS
- OCCUPANCY SENSOR – SEE ELECTRICAL DRAWINGS
- 610mm x 610mm LIGHT FIXTURE – SEE ELECTRICAL DRAWINGS
- 610mm x 1220mm LIGHT FIXTURE – SEE ELECTRICAL DRAWINGS
- ROUND CEILING SURFACE MOUNTED LIGHT FIXTURE – SEE ELECTRICAL DRAWINGS
- RETURN DIFFUSER – SEE MECHANICAL DRAWINGS
- SUPPLY DIFFUSER – SEE MECHANICAL DRAWINGS
- MOISTURE RESISTANT GYPSUM BOARD
- 3HR RATED CEILING: PRECAST CONCRETE ON FIRE PROOFED STEEL BEAMS.
- 610mm X 610mm ACOUSTICAL CEILING PANEL SUSPENDED FROM SUSPENDED GYPSUM WALL BOARD CEILING SYSTEM.
- 610mm X 610mm ACOUSTICAL CEILING PANEL
- SURFACE MOUNTED DOUBLE FACE EXIT SIGNS – SEE ELECTRICAL DRAWINGS
- LED WALL PACKS – SEE ELECTRICAL DRAWINGS

GRAPHIC SCALE




APPROVED: _____
FOR COMMANDER NAVFAC
ACTIVITY
D. EVANS VIA EMAIL
SATISFACTORY TO: _____ DATE: 01/15/2026
DES: PAK PM/DM: PAK
BRANCH MANAGER: MJD/ATP
DES PROD DIR: KMC
FIRE PROTECTION ENGINEER: WBF DSN

DEPARTMENT OF THE NAVY
NAVAL FACILITIES ENGINEERING SYSTEMS COMMAND
PLANNING, DESIGN AND CONSTRUCTION
NAVFAC
VARIOUS LOCATIONS
VARIOUS LOCATIONS
JOINT MARITIME FACILITY
REFLECTED CEILING PLAN


SCALE: AS NOTED
APPROVED NO.: 1838720
CONSTR. CONTR. NO.:
NAVFAC DRAWING NO.: 14157121
SHEET 59 OF 170
A-106

FILE NAME: Y:\OCONUS\MultipleSites\2026_1783264_P1360_JMFB\B_Design\DWG\Sheet\08_ARCH\PT1360_1783264_A107.dwg LAYOUT NAME: A-107 ROOF PLAN PLOTTED: Wednesday, January 21, 2026 - 8:30am USER: paula.keller1

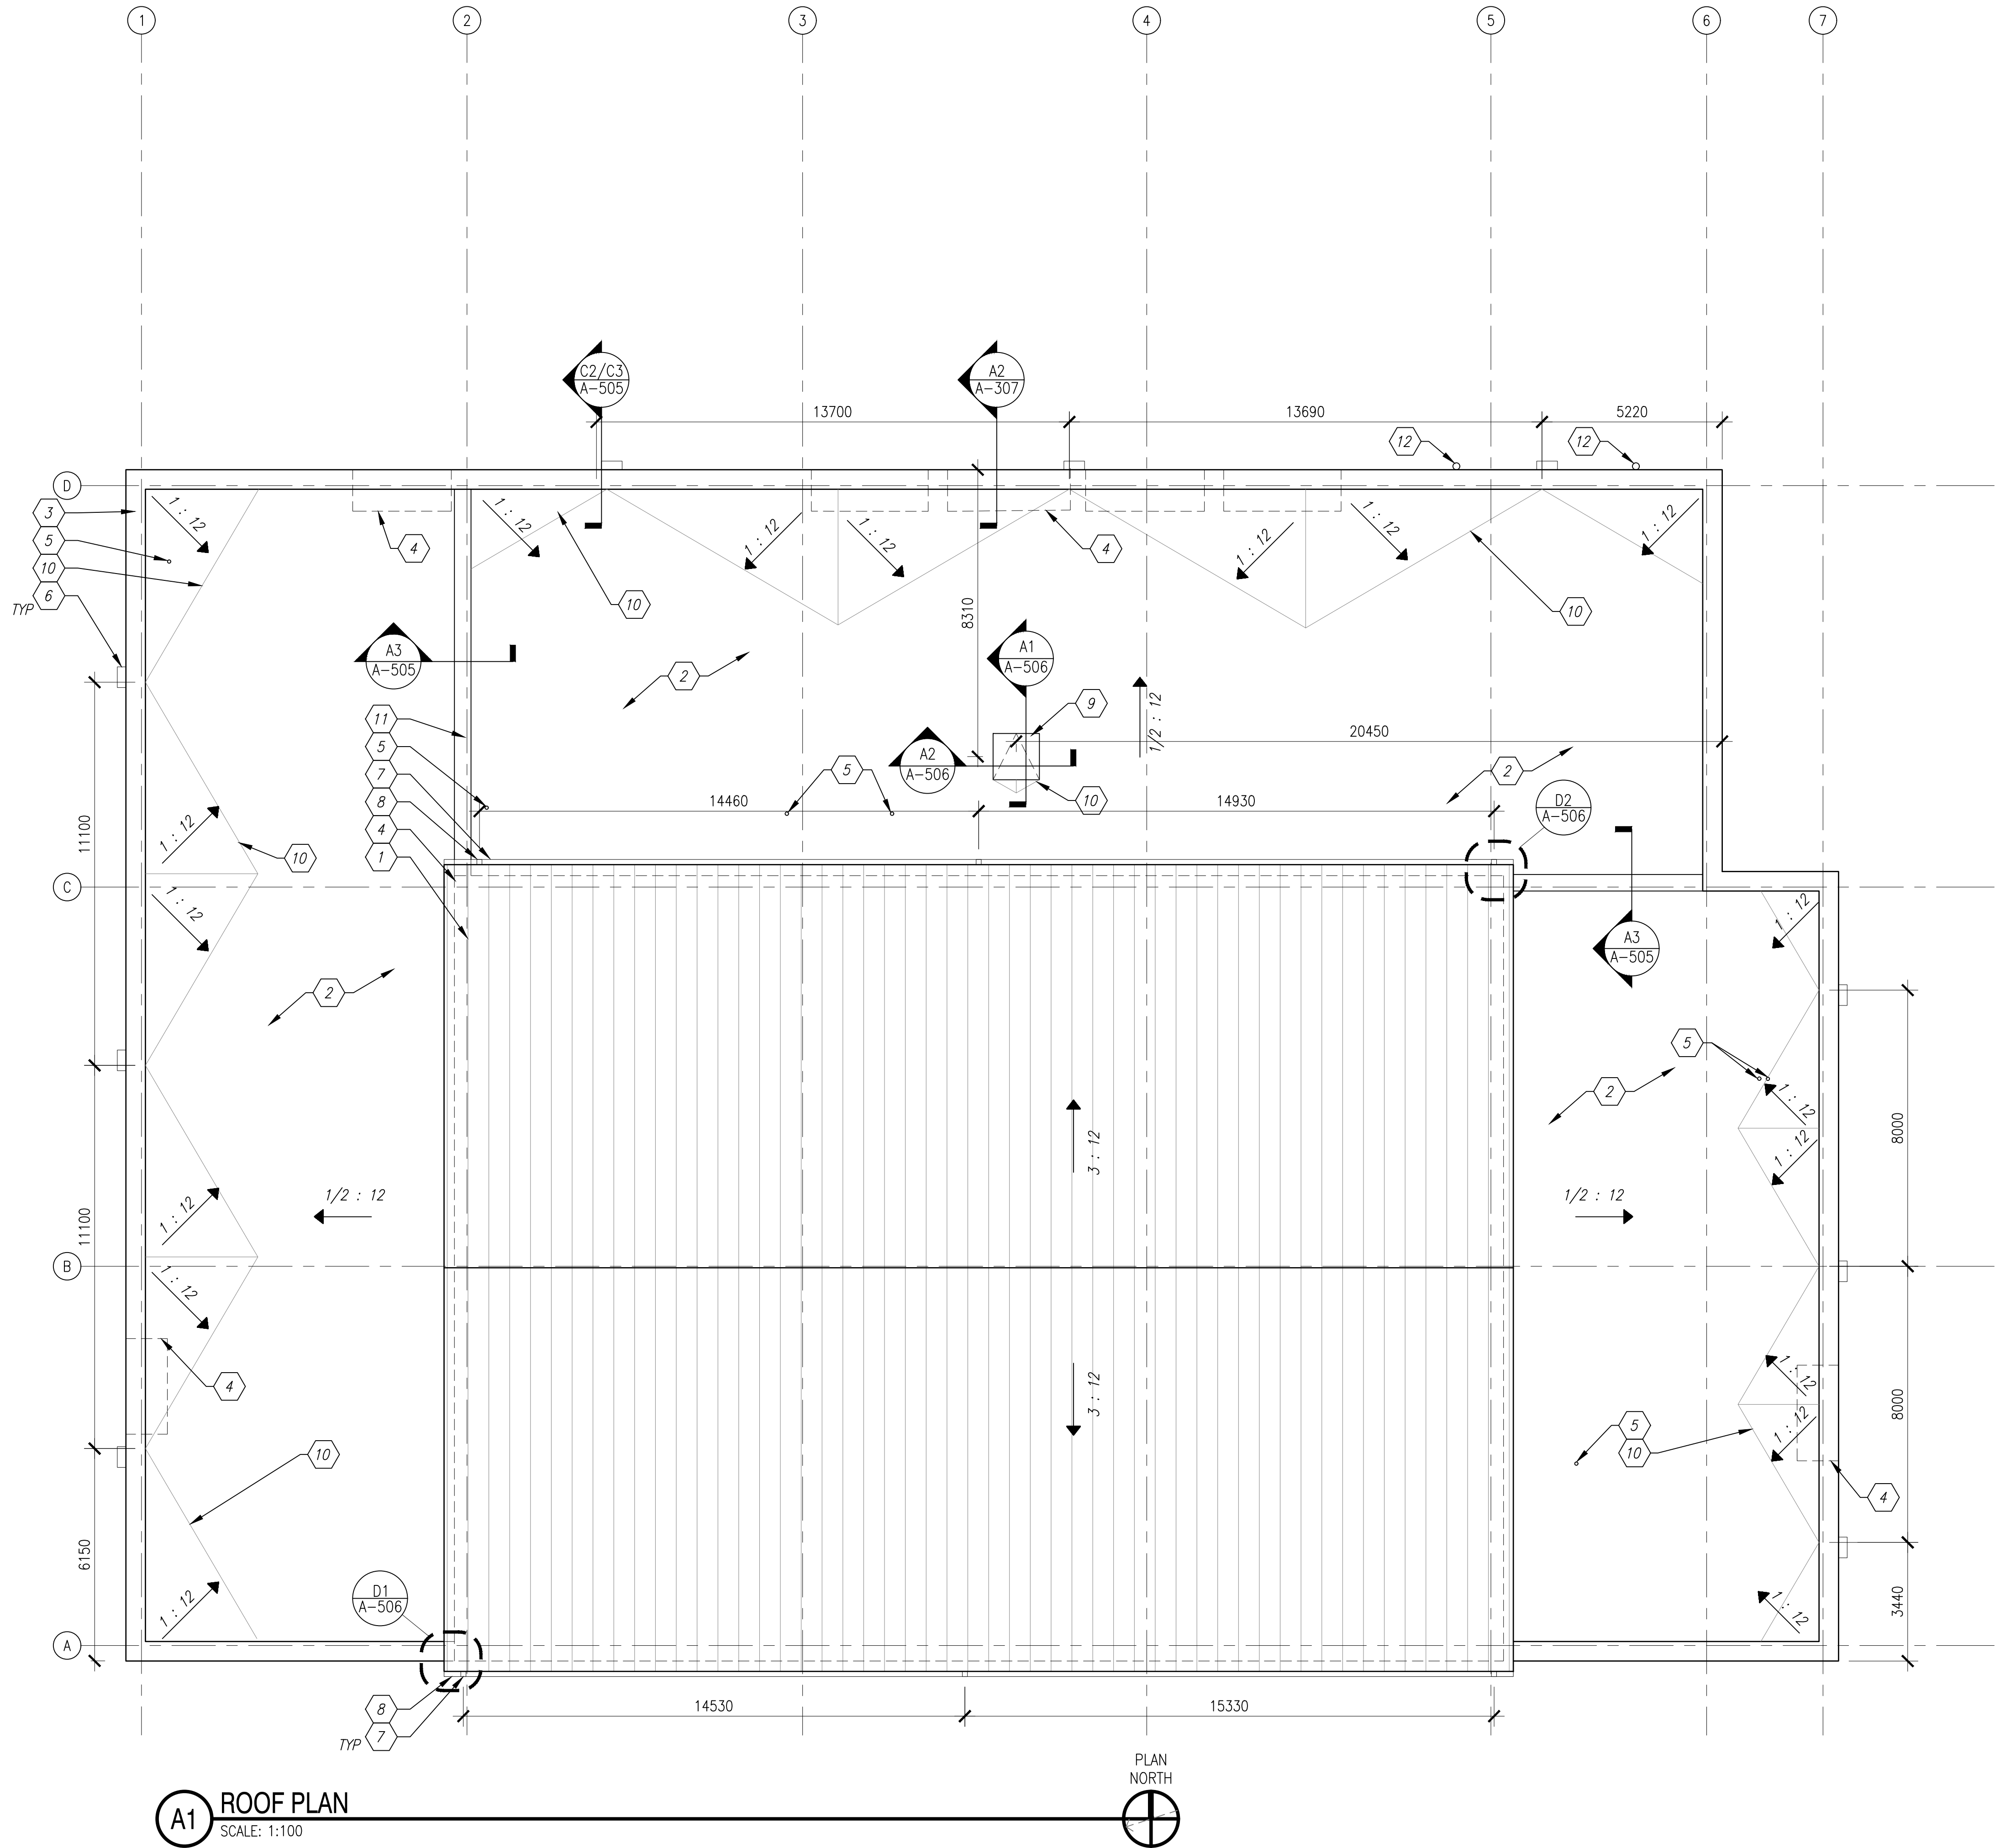

GENERAL SHEET NOTES

- REFER TO SHEET A-001 FOR ARCHITECTURAL LEGEND AND ABBREVIATIONS.
- REFER TO SHEET A-101 FOR KEYNOTES THIS SHEET.
- REFER TO SHEET A-605 FOR PARTITION SCHEDULE.
- REFER TO SHEET A-606 FOR LOUVER SCHEDULE.
- SEE INTERIOR 'I' SERIES SHEETS FOR FINISH, FURNITURE AND EQUIPMENT LAYOUTS.
- PROVIDE FIRE RETARDANT TREATED WOOD BLOCKING FOR MOUNTING OF GRAB BARS, WALL MOUNTED CABINETS, AV OR IT EQUIPMENT, AND WHERE NECESSARY FOR PROPER ATTACHMENT OF ITEMS. SECURELY ATTACH BLOCKING TO METAL STUD FLANGES. COORDINATE EXACT LOCATION AND QUANTITY OF BLOCKING WITH EQUIPMENT REQUIRING REINFORCEMENT.
- PROVIDE PLYWOOD BACKBOARDS WHERE REQUIRED FOR COMMUNICATIONS EQUIPMENT. ALL EXPOSED EDGES OF BACKBOARD SHALL BE PAINTED ON FIVE SIDES WITH A FIRE RETARDANT PAINT. SEE ELECTRICAL/TELECOM DRAWINGS FOR ADDITIONAL INFORMATION.
- FINISH FLOOR ELEVATION IS 0.00mm UNLESS OTHERWISE NOTED.

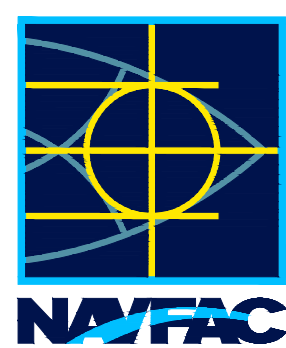

APPROVED
FOR COMMANDER NAVFAC
ACTIVITY
D. EVANS VIA EMAIL
SATISFACTORY TO DATE 01/15/2026
DES PAK DRW PAK LHM JHR
PM/DM MJD/ATP
BRANCH MANAGER KMC
DES PROD DIR WBF
FIRE PROTECTION ENGINEER DSN

DEPARTMENT OF THE NAVY
NAVAL FACILITIES ENGINEERING SYSTEMS COMMAND
NAVAL FACILITIES ENGINEERING SYSTEMS COMMAND - ATLANTIC
PLANNING, DESIGN AND CONSTRUCTION
VARIOUS LOCATIONS
VARIOUS LOCATIONS
JOINT MARITIME FACILITY
ROOF PLAN

SCALE: AS NOTED
APPROVED NO.: 1838720
CONSTR. CONTR. NO.
NAVFAC DRAWING NO. 14157122
SHEET 60 OF 170
A-107

FILE NAME: Y:\OCONUS\MultipleSites\2026_1783264_P1360_IAMF\B_Design\DWG\Sheet\08_ARCH\PT1360_1783264_2026.dwg LAYOUT NAME: A-205 ELEVATIONS PLOTTED: Wednesday, January 21, 2026 - 8:30am USER: paula.keller1

D

C

B

A

B1 NORTH ELEVATION
SCALE: 1:100

A1 WEST ELEVATION
SCALE: 1:100

TOP OF STEEL
9450.00 mm



TOP OF PARAPET
5650.00 mm

FINISHED FLOOR
00.00 mm

TOP OF STEEL
9450.00 mm

TOP OF PARAPET
5650.00 mm

FINISHED FLOOR
00.00 mm

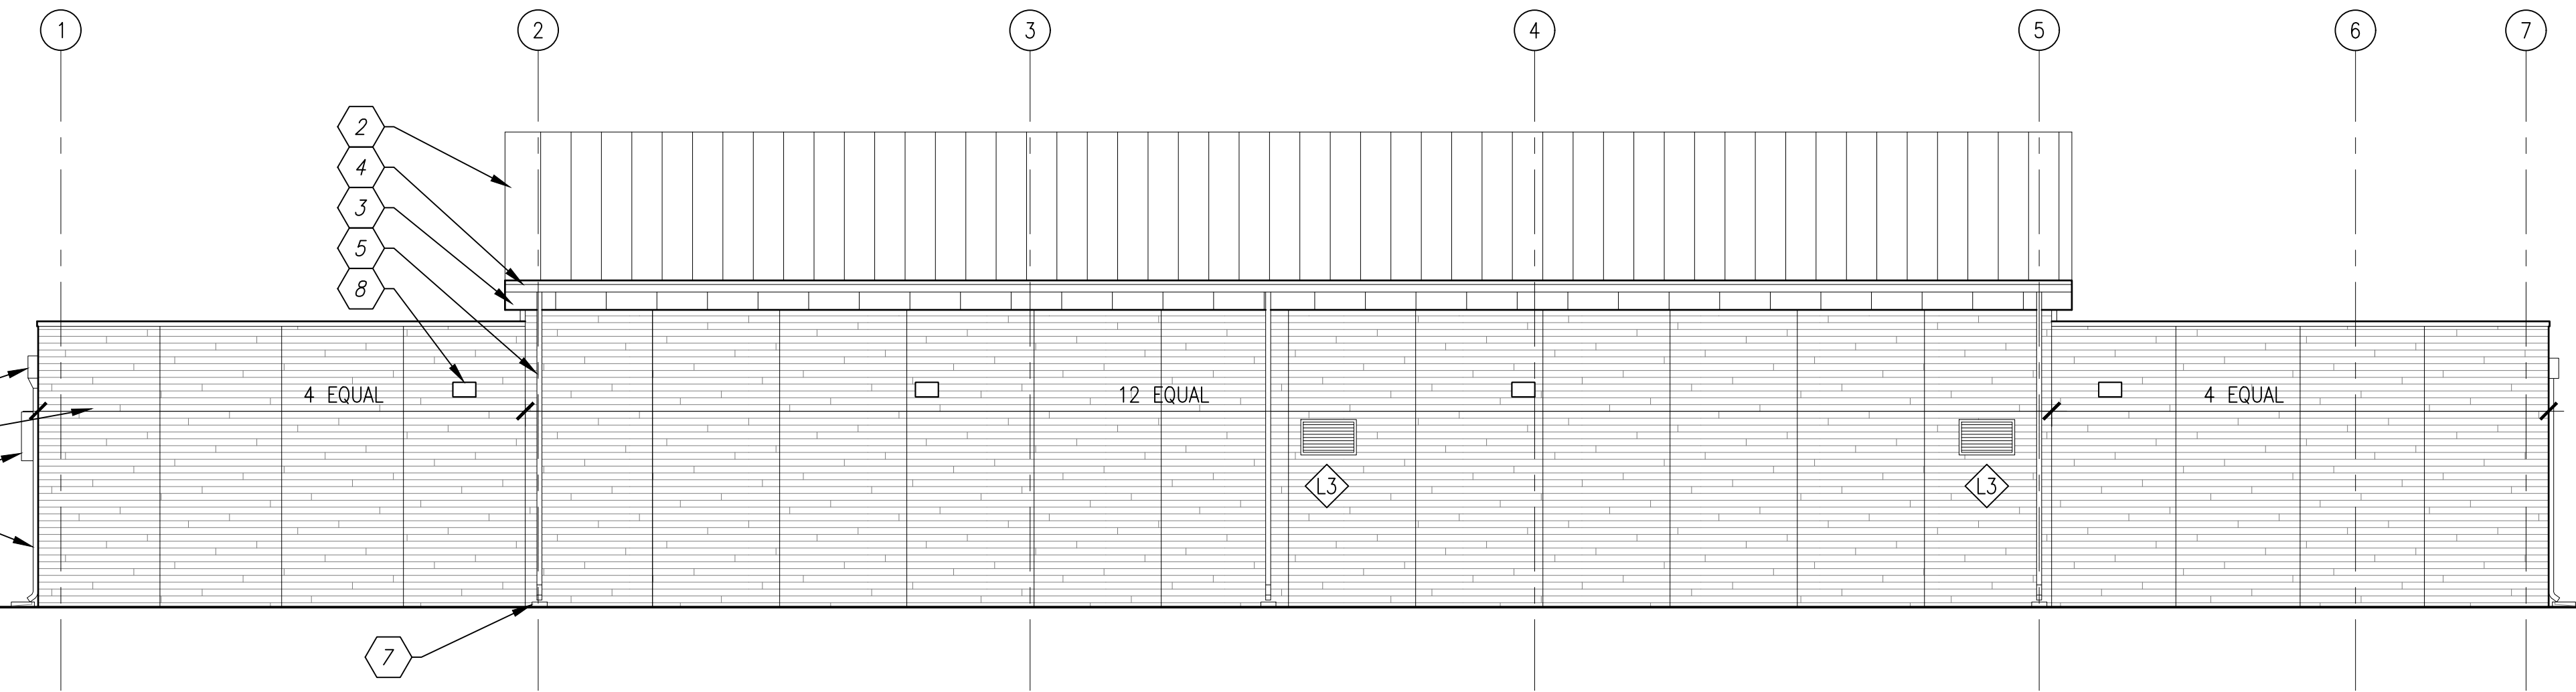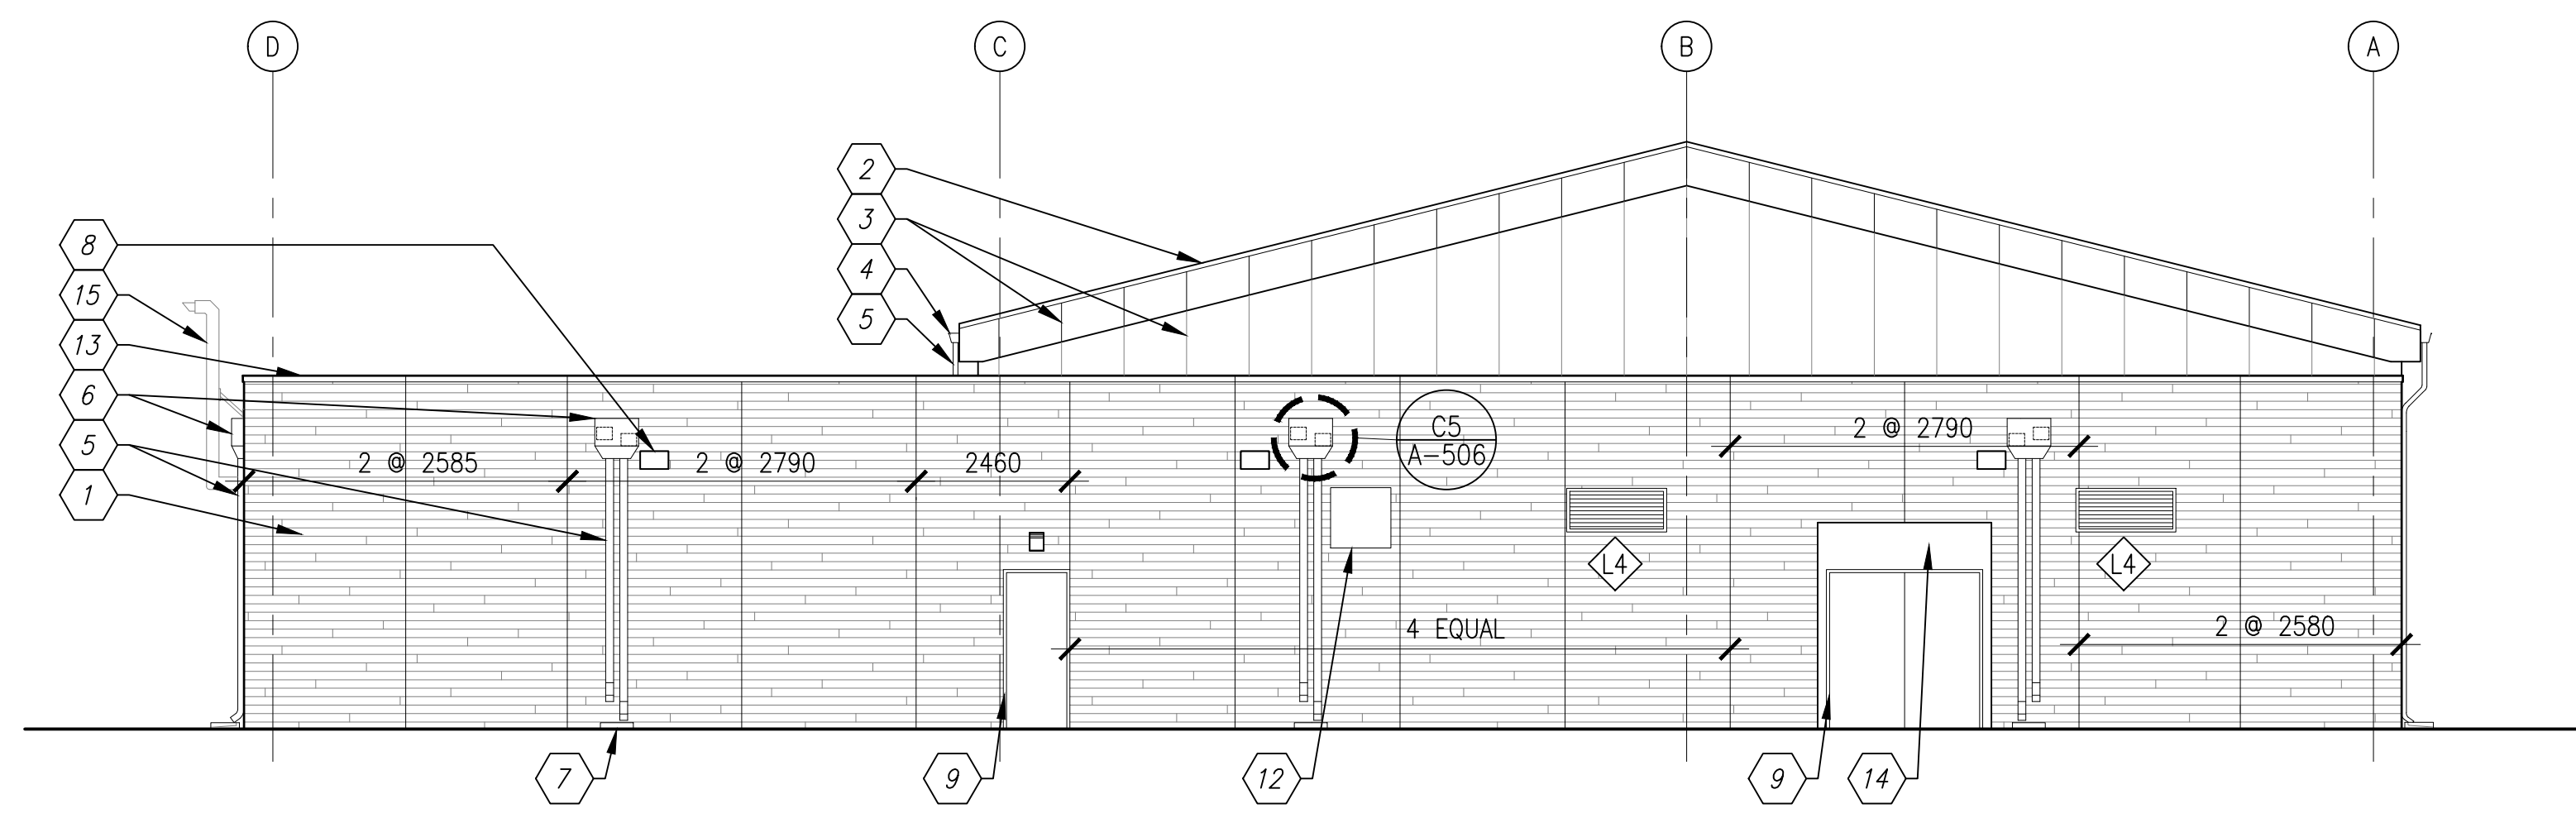

GENERAL SHEET NOTES

- A. REFER TO SHEET A-001 FOR ARCHITECTURAL LEGEND AND ABBREVIATIONS.
- B. REFER TO SHEET A-201 FOR KEYNOTES THIS SHEET.
- C. REFER TO SHEET A-606 FOR WINDOW AND LOUVER SCHEDULE
- D. PROVIDE FIRE RETARDANT TREATED WOOD BLOCKING FOR MOUNTING OF GRAB BARS, WALL MOUNTED CABINETS, AV OR IT EQUIPMENT, AND WHERE NECESSARY FOR PROPER ATTACHMENT OF ITEMS. SECURELY ATTACH BLOCKING TO METAL STUD FLANGES. COORDINATE EXACT LOCATION AND QUANTITY OF BLOCKING WITH EQUIPMENT REQUIRING REINFORCEMENT.
- E. PROVIDE PLYWOOD BACKBOARDS WHERE REQUIRED FOR COMMUNICATIONS EQUIPMENT. ALL EXPOSED EDGES OF BACKBOARD SHALL BE PAINTED ON FIVE SIDES WITH A FIRE RETARDANT PAINT. SEE ELECTRICAL/TELECOM DRAWINGS FOR ADDITIONAL INFORMATION
- F. FINISH FLOOR ELEVATION IS 0.00mm UNLESS OTHERWISE NOTED.
- G. COORDINATE ALL OPENINGS THROUGH INSULATED STRUCTURAL PRECAST SANDWICH PANELS PRIOR TO MANUFACTURING.



APPROVED

FOR COMMANDER NAVFAC

ACTIVITY

D. EVANS VIA EMAIL

SATISFACTORY TO DATE 01/15/2026

DES PAK DRW PAK

PM/DM MJD/ATP

BRANCH MANAGER KMC

DES PROD DIR WBF

FIRE PROTECTION ENGINEER DSN

DEPARTMENT OF THE NAVY
NAVAL FACILITIES ENGINEERING SYSTEMS COMMAND
NAVAL FACILITIES ENGINEERING SYSTEMS COMMAND - ATLANTIC
PLANNING, DESIGN AND CONSTRUCTION

VARIOUS LOCATIONS
VARIOUS LOCATIONS
VARIOUS LOCATIONS

JOINT MARITIME FACILITY
ELEVATIONS

GRAPHIC SCALE



SCALE: AS NOTED

APPROVED NO.: 1838720

CONSTR. CONTR. NO.


NAVFAC DRAWING NO. 14157124

SHEET 62 OF 170


A-205

FILE NAME: Y:\OCONUS\MultipleSites\2026_1783264_P1360_JAMFAB_Design\DWG\Sheet\08_ARCH\PT1360_1783264_2026.dwg LAYOUT NAME: A-206 ELEVATIONS PLOTTED: Wednesday, January 21, 2026 - 6:30am USER: paula.keller1

B1 SOUTH ELEVATION
SCALE: 1:100

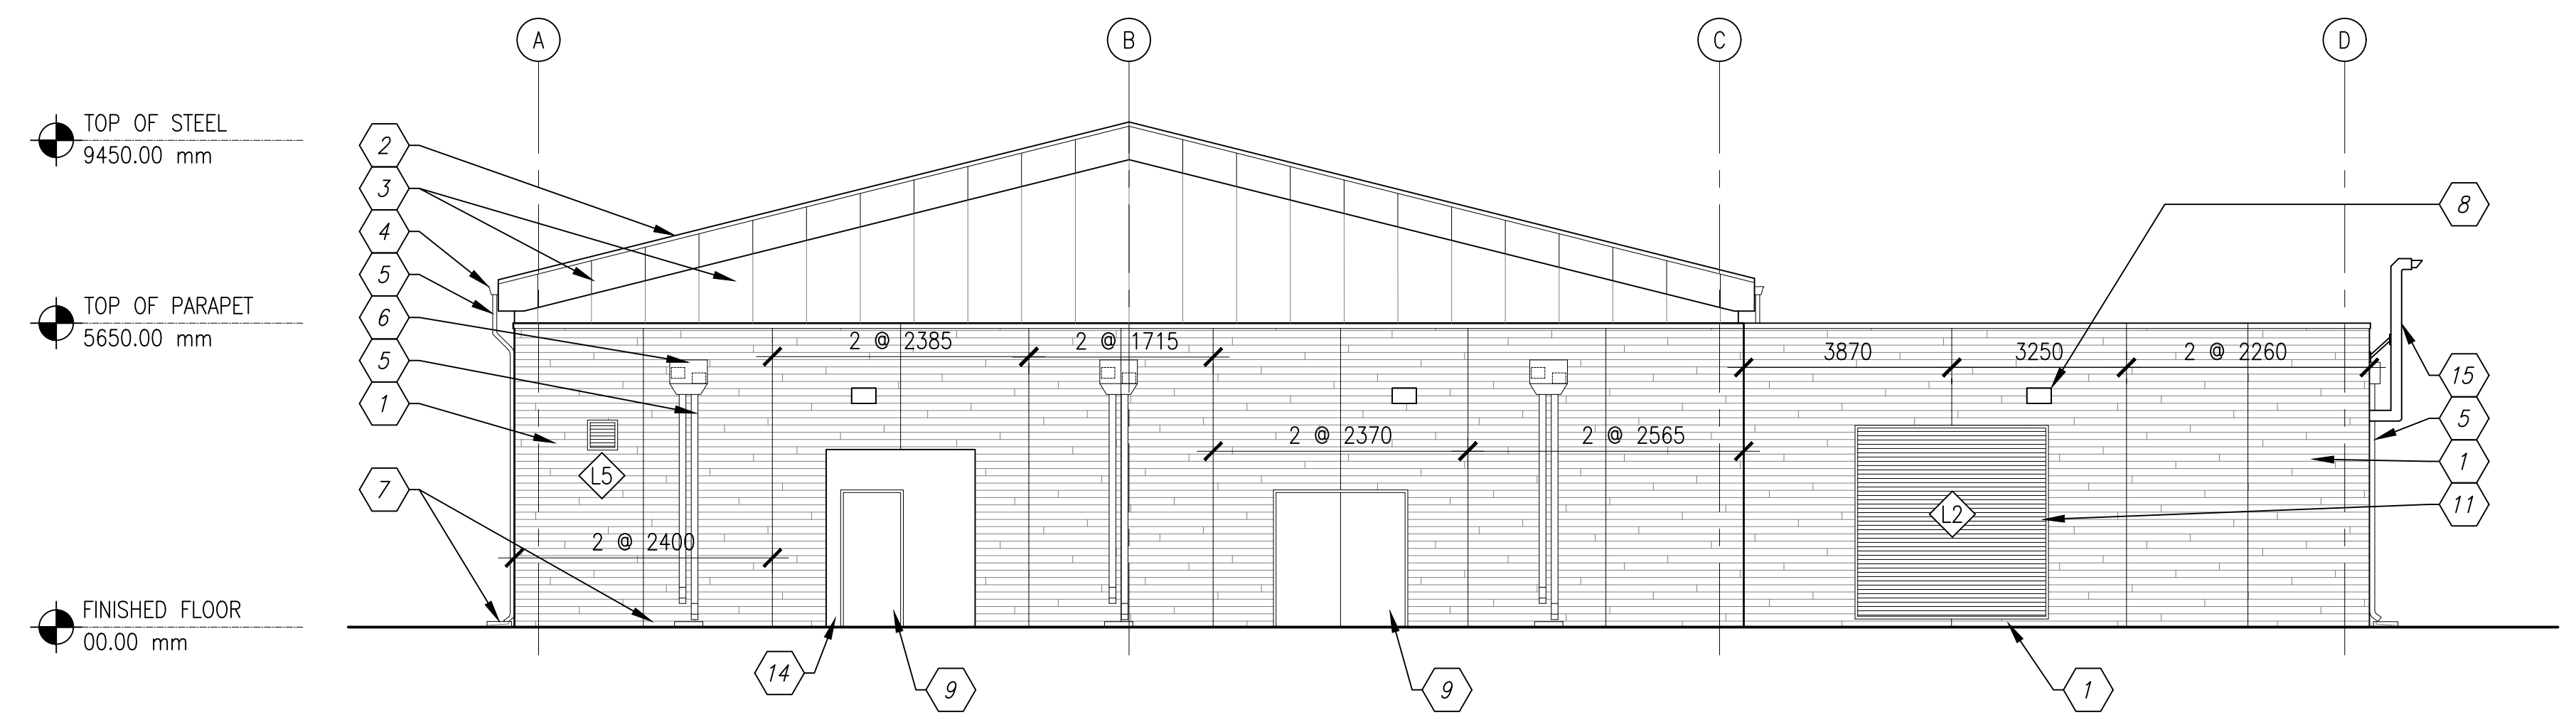

A1 EAST ELEVATION
SCALE: 1:100

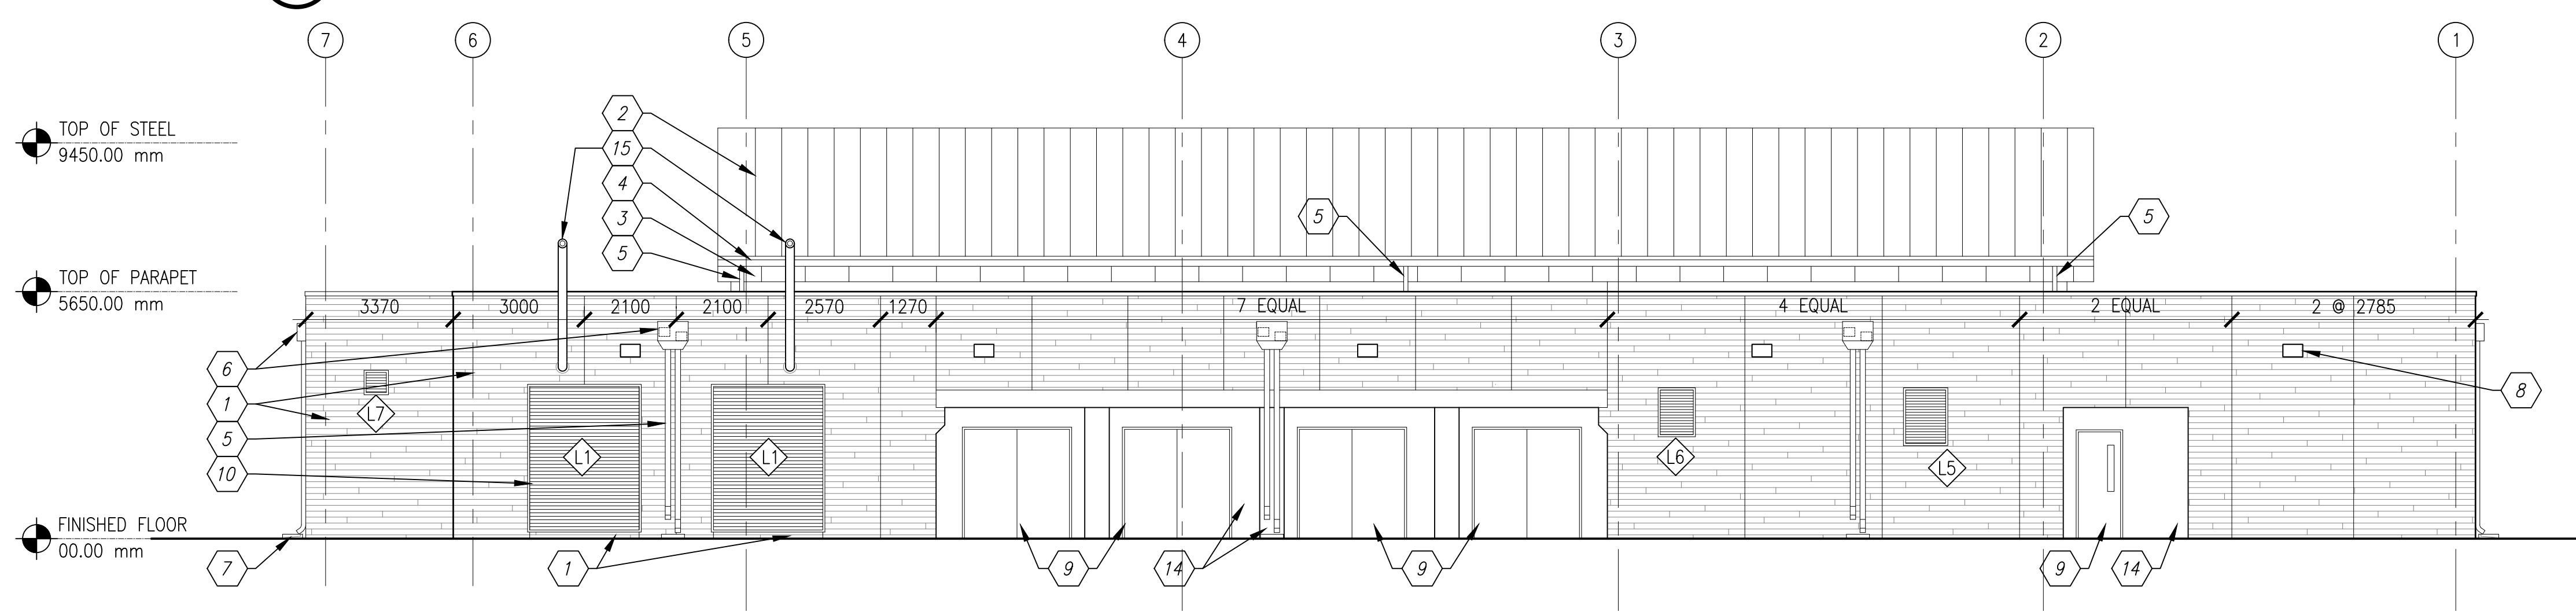

GENERAL SHEET NOTES


- A. REFER TO SHEET A-001 FOR ARCHITECTURAL LEGEND AND ABBREVIATIONS.
- B. REFER TO SHEET A-201 FOR KEYNOTES THIS SHEET.
- C. REFER TO SHEET A-606 FOR WINDOW AND LOUVER SCHEDULE
- D. PROVIDE FIRE RETARDANT TREATED WOOD BLOCKING FOR MOUNTING OF GRAB BARS, WALL MOUNTED CABINETS, AV OR IT EQUIPMENT, AND WHERE NECESSARY FOR PROPER ATTACHMENT OF ITEMS. SECURELY ATTACH BLOCKING TO METAL STUD FLANGES. COORDINATE EXACT LOCATION AND QUANTITY OF BLOCKING WITH EQUIPMENT REQUIRING REINFORCEMENT.
- E. PROVIDE PLYWOOD BACKBOARDS WHERE REQUIRED FOR COMMUNICATIONS EQUIPMENT. ALL EXPOSED EDGES OF BACKBOARD SHALL BE PAINTED ON FIVE SIDES WITH A FIRE RETARDANT PAINT. SEE ELECTRICAL/TELECOM DRAWINGS FOR ADDITIONAL INFORMATION
- F. FINISH FLOOR ELEVATION IS 0.00mm UNLESS OTHERWISE NOTED.
- G. COORDINATE ALL OPENINGS THROUGH INSULATED STRUCTURAL PRECAST SANDWICH PANELS PRIOR TO MANUFACTURING.



APPROVED
FOR COMMANDER NAVFAC
ACTIVITY
D. EVANS VIA EMAIL
SATISFACTORY TO DATE 01/15/2026
DES PAK DRW PAK CHK JHR
PM/DM MJD/ATP
BRANCH MANAGER KMC
DES PROD DIR WBF
FIRE PROTECTION ENGINEER DSN

DEPARTMENT OF THE NAVY	NAVAL FACILITIES ENGINEERING SYSTEMS COMMAND	NAVAL FACILITIES ENGINEERING SYSTEMS COMMAND - ATLANTIC	VARIOUS LOCATIONS
PLANNING, DESIGN AND CONSTRUCTION	VARIOUS LOCATIONS	VARIOUS LOCATIONS	VARIOUS LOCATIONS
JOINT MARITIME FACILITY			
ELEVATIONS			

GRAPHIC SCALE

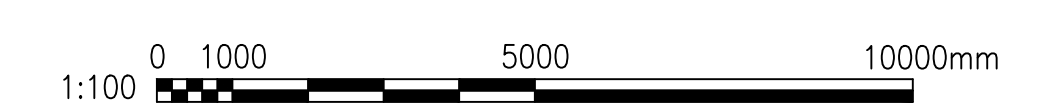

SCALE: AS NOTED
APPROVED NO. 1838720
CONSTR. CONTR. NO.
NAVFAC DRAWING NO. 14157125
SHEET 63 OF 170
A-206

(FOR SHEET A-305)

INSULATED STRUCTURAL PRECAST CONCRETE SANDWICH PANELS
(MIN RSI 5.46)

INTERIOR WALL FURRING, SEE PARTITION SCHEDULE

STANDING SEAM METAL ROOF PANEL ON HIGH TEMP ICE AND WATER SHIELD ON 15MM GLASS MATT GYPSUM ROOF COVER BOARD, ON MIN RSI 8.805 RIGID INSULATION ON VAPOR BARRIER, ON 15MM GLASS MAT GYP PROTECTION BOARD ON CORRUGATED METAL DECKING.

SBS COLD-APPLIED MODIFIED BITUMEN ROOF ON 15MM GLASS
MATT GYPSUM ROOF COVER BOARD, ON MIN RSI 8.805 RIGID
INSULATION ON VAPOR BARRIER, ON 15MM GLASS MAT GYP
PROTECTION BOARD ON CORRUGATED METAL DECKING.

100MM FABRICATED WALL PANEL ASSEMBLY WITH SMOOTH
TEXTURE. MIN RSI 5.46

INSULATED STRUCTURAL PRECAST CONCRETED SANDWICH PANELS

ELASTOMERIC COATING ON 15.875MM (5/8 IN) TYPE X GLASS
MATT GYPSUM COVERBOARD ON 100MM RIGID INSULATION.

RAISED ACCESS FLOORING

CONTINUOUS WATERPROOFING APPLIED TO BELOW GRADE FACE
OF PRECAST CONCRETE PANELS.

STEEL STRUCTURE

CONCRETE FLOOR SLAB


CONCRETE FOUNDATION

PERIMETER FOUNDATION INSULATION, MIN RSI 1.82.
EXTEND MIN 1200 MM.

SUSPENDED ACOUSTICAL CEILING GRID, AS SCHEDULED.

PASSIVE BELOW SLAB RADON MITIGATION SYSTEM. REFER TO STRUCTURAL AND PLUMBING DRAWINGS.

STRUCTURAL PRECAST CONCRETE

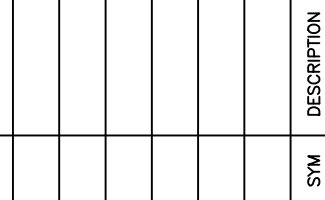

A-301

FILE NAME: Y:\CONUS\MultipleSites\2024_1783264_P1360_IAMFB_B_Design\DWG\Sheet\08_ARCH\PT1360_1783264_A305.dwg LAYOUT NAME: A-305 BUILDING SECTIONS PLOTTED: Wednesday, January 21, 2026 - 8:30am USER: paul.akef1

D

C

B

A

1

2


3

4

5

GENERAL SHEET NOTES

- REFER TO SHEET A-001 FOR ARCHITECTURAL LEGEND AND ABBREVIATIONS.
- REFER TO SHEET A-605 FOR PARTITION SCHEDULE.
- REFER TO SHEET A-301 FOR KEYNOTES THIS SHEET.
- SEE INTERIOR 'I' SERIES SHEETS FOR FINISH, FURNITURE AND EQUIPMENT LAYOUTS
- PROVIDE FIRE RETARDANT TREATED WOOD BLOCKING FOR MOUNTING OF GRAB BARS, WALL MOUNTED CABINETS, AV OR IT EQUIPMENT, AND WHERE NECESSARY FOR PROPER ATTACHMENT OF ITEMS. SECURELY ATTACH BLOCKING TO METAL STUD FLANGES. COORDINATE EXACT LOCATION AND QUANTITY OF BLOCKING WITH EQUIPMENT REQUIRING REINFORCEMENT.
- PROVIDE PLYWOOD BACKBOARDS WHERE REQUIRED FOR COMMUNICATIONS EQUIPMENT. ALL EXPOSED EDGES OF BACKBOARD SHALL BE PAINTED ON FIVE SIDES WITH A FIRE RETARDANT PAINT. SEE ELECTRICAL/TELECOM DRAWINGS FOR ADDITIONAL INFORMATION
- FINISH FLOOR ELEVATION IS 0.00mm UNLESS OTHERWISE NOTED.


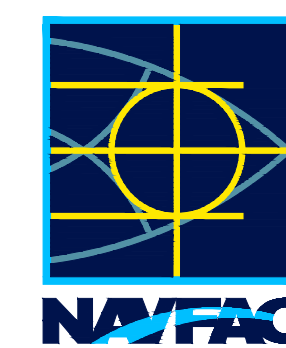


D

C

B

A

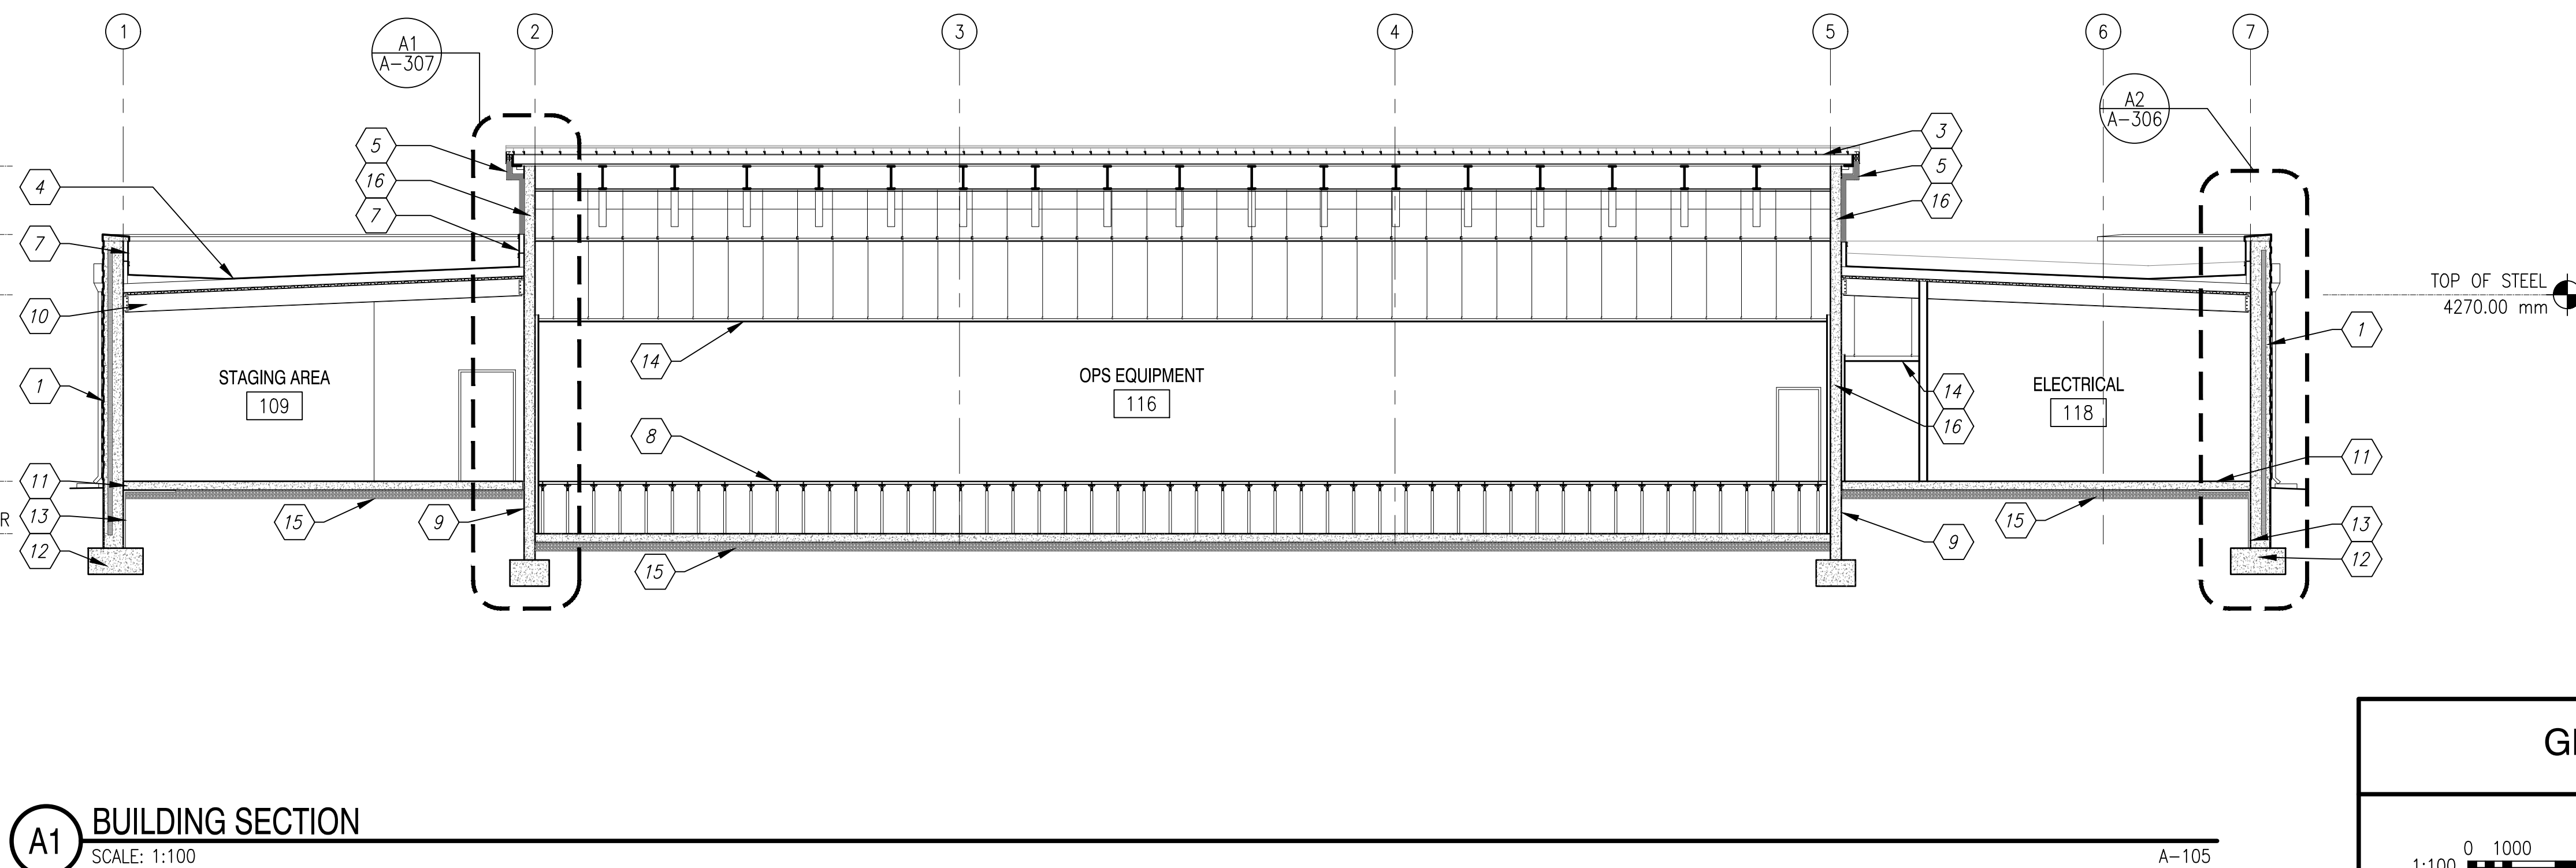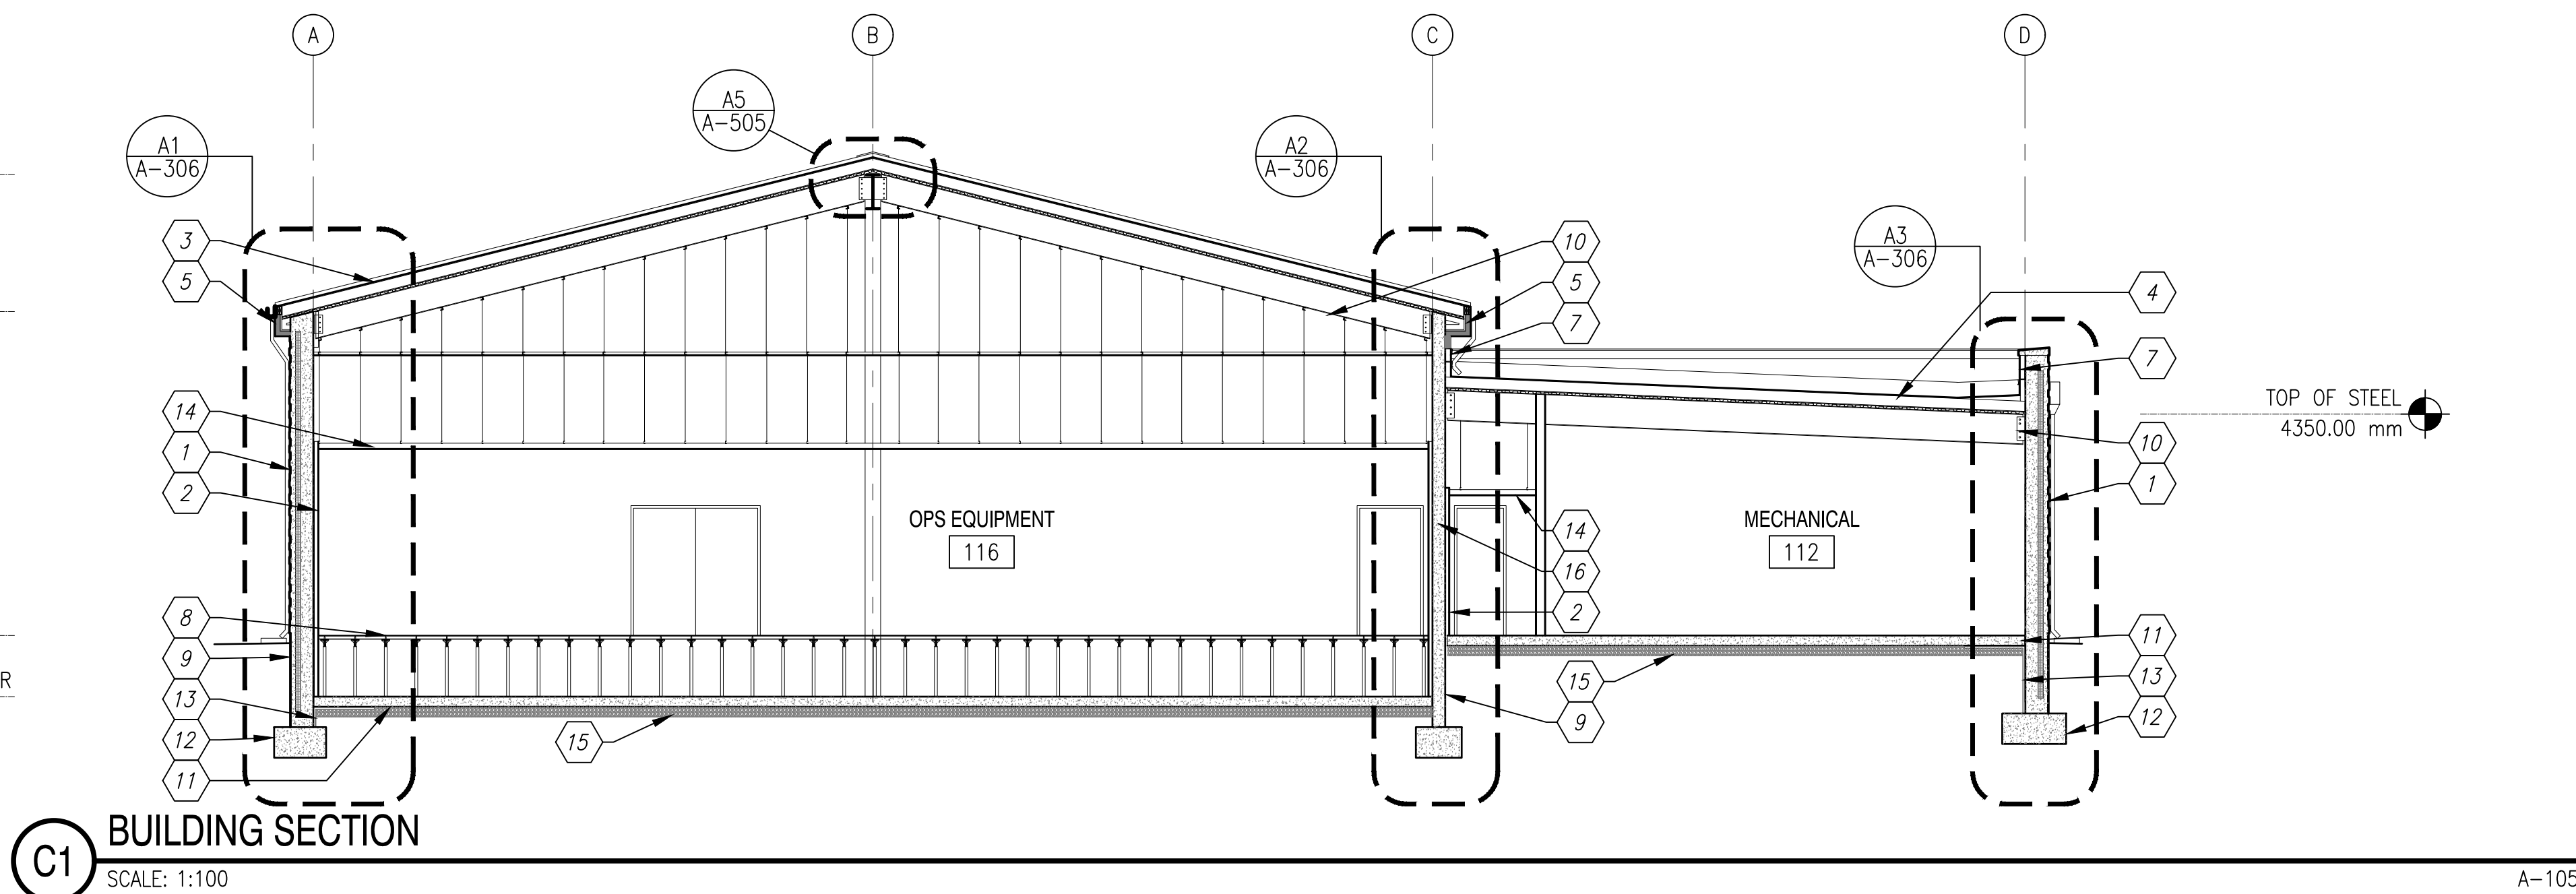

GRAPHIC SCALE

1:100 0 1000 5000 10000mm

APPROVED

FOR COMMANDER NAVFAC

ACTIVITY

D. EVANS VIA EMAIL

SATISFACTORY TO DATE 01/15/2026

DES PAK DRW PAK CHK JHR

PM/DM MJD/ATP

BRANCH MANAGER KMC

DES PROD DIR WBF

FIRE PROTECTION ENGINEER DSN

NAVAL FACILITIES ENGINEERING SYSTEMS COMMAND

NAVAL FACILITIES ENGINEERING SYSTEMS COMMAND - ATLANTIC

PLANNING, DESIGN AND CONSTRUCTION

VARIOUS LOCATIONS

VARIOUS LOCATIONS

VARIOUS LOCATIONS

JOINT MARITIME FACILITY

BUILDING SECTIONS

SCALE: AS NOTED

APPROVED NO.: 1838720




CONSTR. CONTR. NO.

NAVFAC DRAWING NO. 14157128

SHEET 66 OF 170

A-305

FILE NAME: Y:\CONUS\MultipleSites\2026_1783264_P1360_JAMFAB_Design\DWG\Sheet\08_ARCH\PT1360_1783264_A306-A307.dwg LAYOUT NAME: A-306 WALL SECTIONS PLOTTED: Wednesday, January 21, 2026 - 8:30am USER: paula.keller1

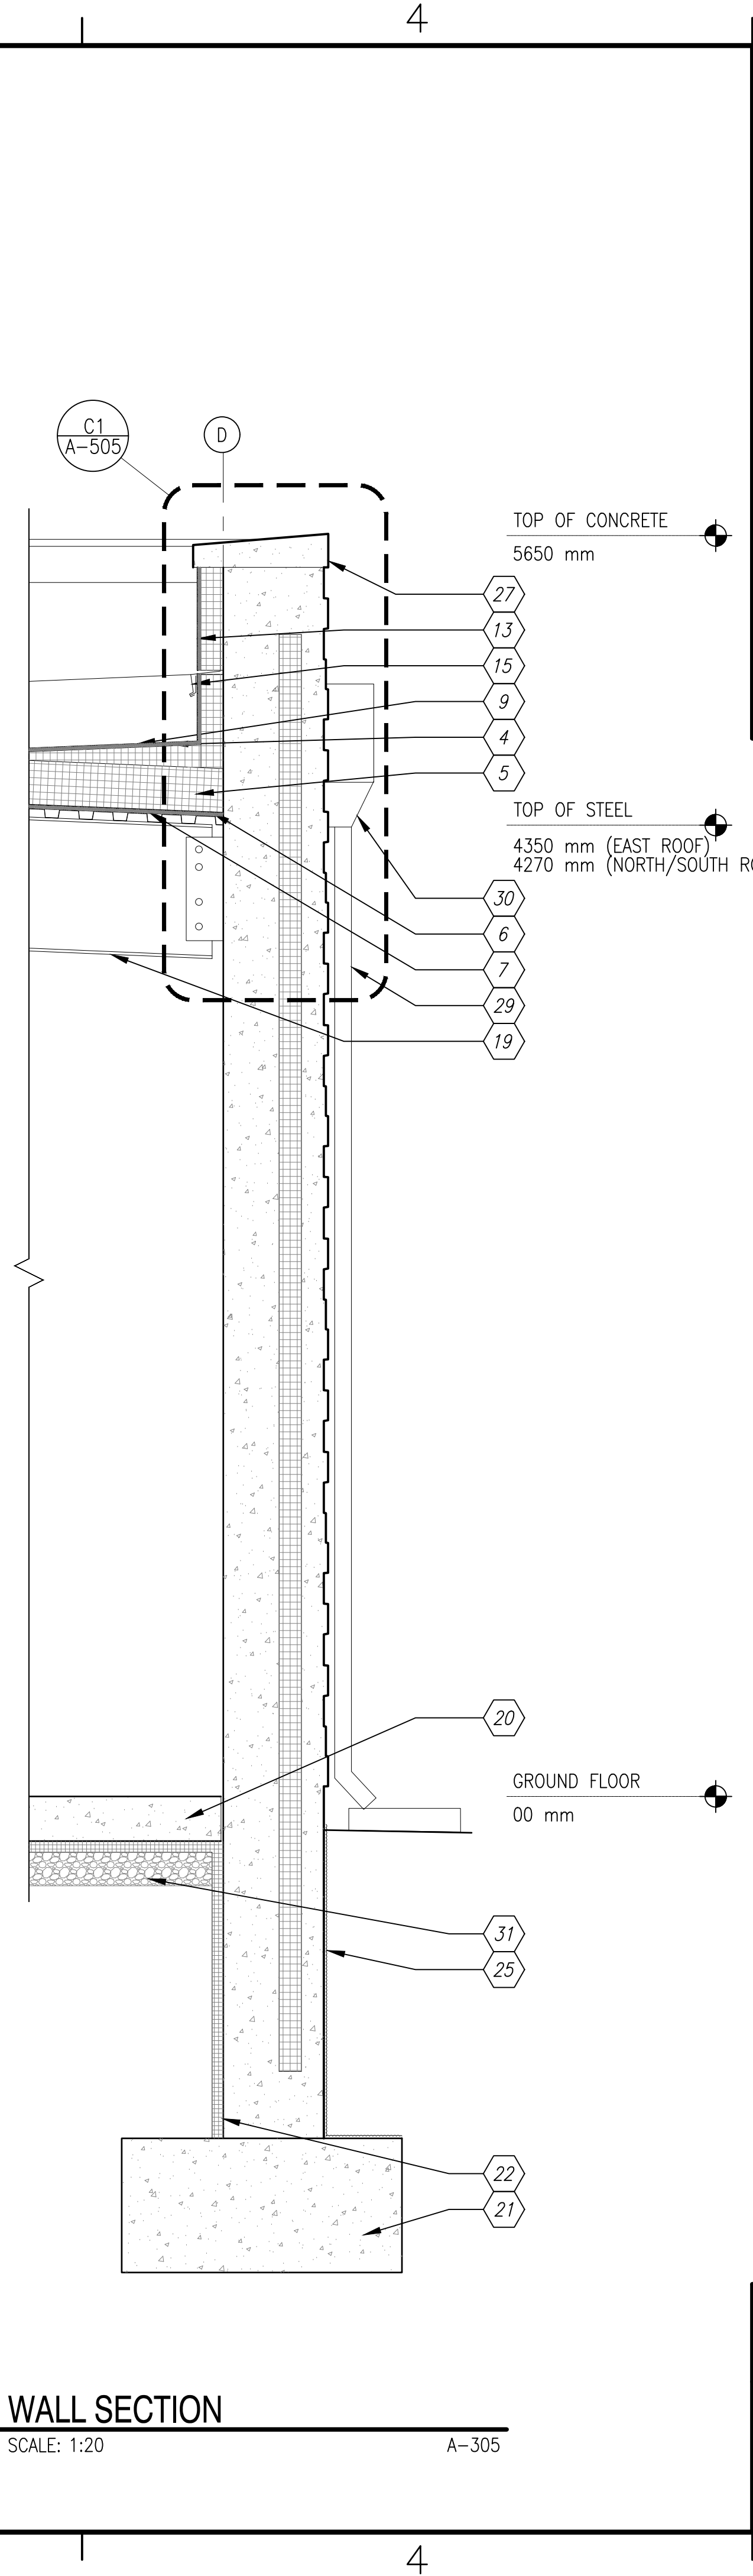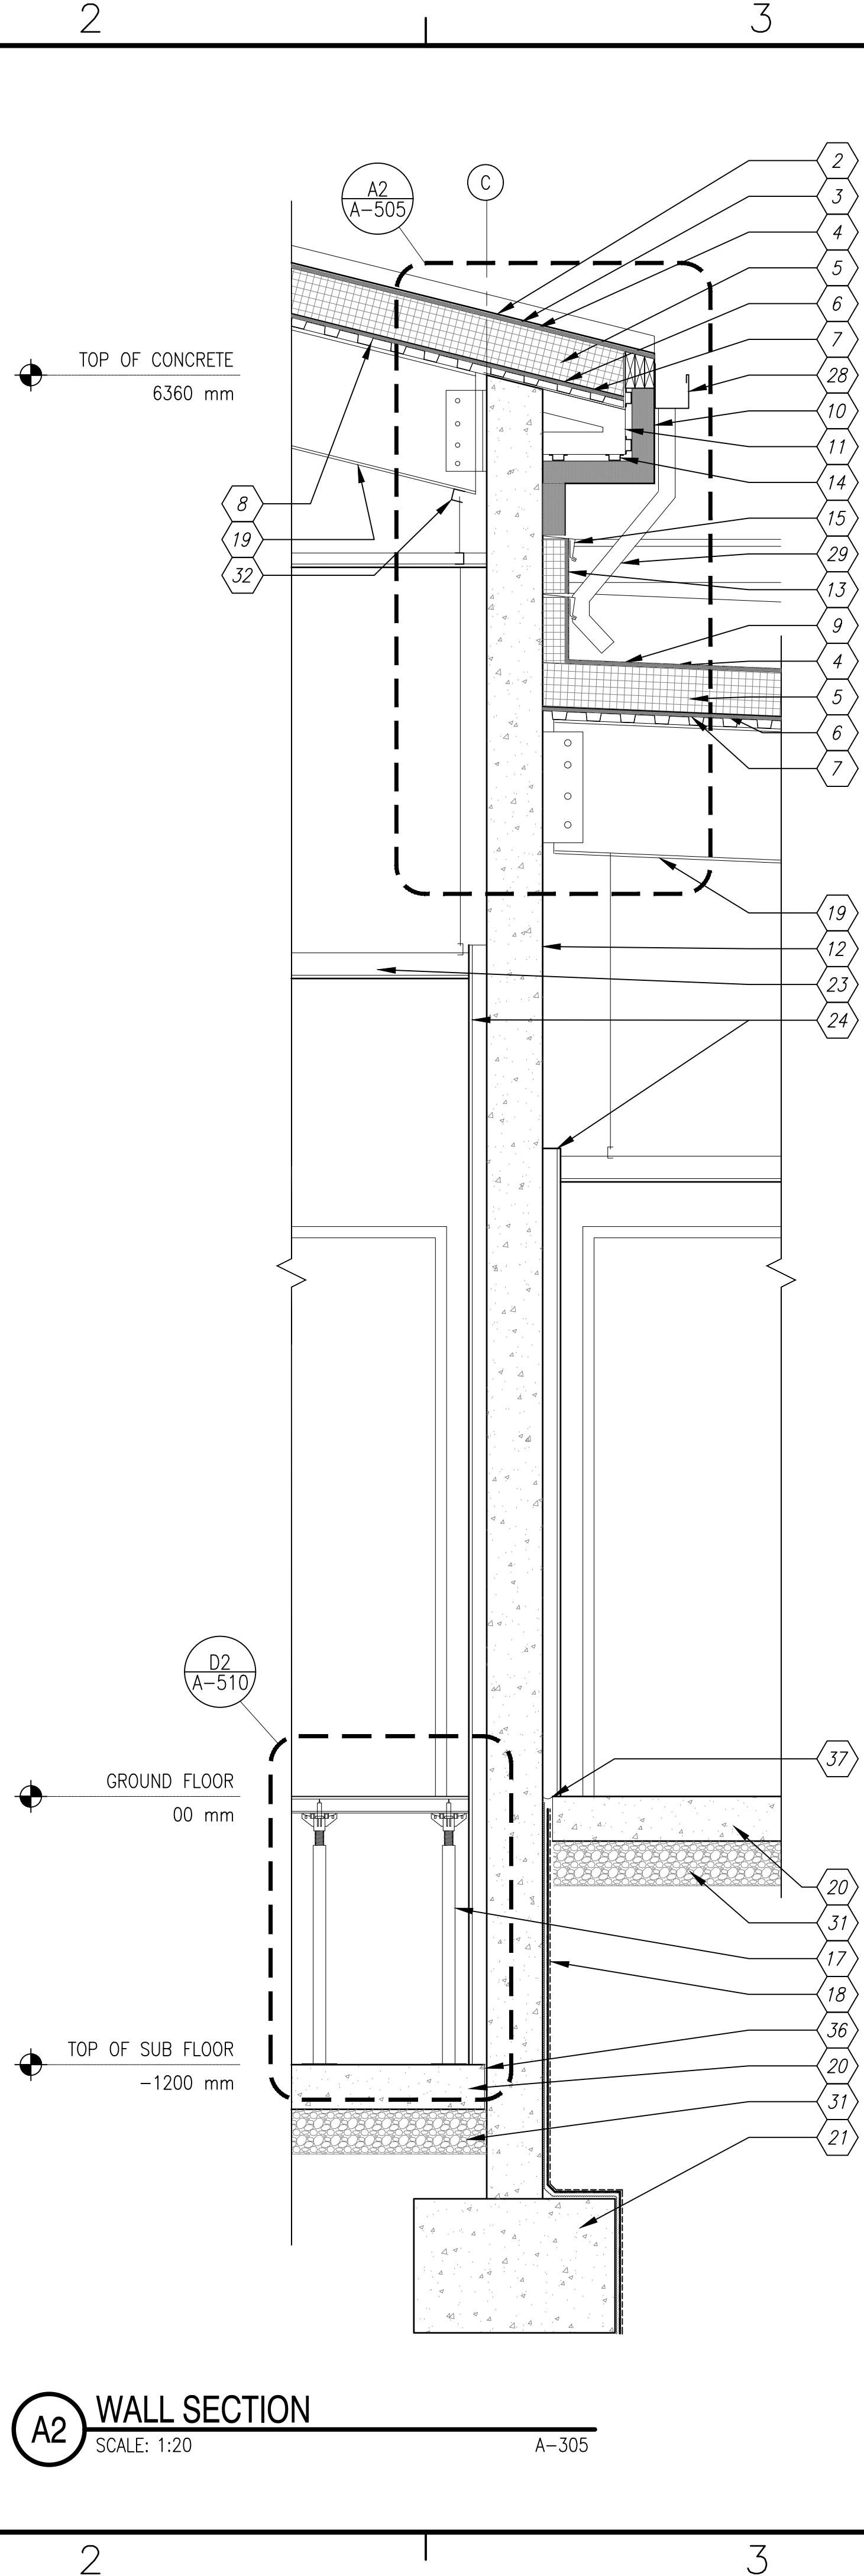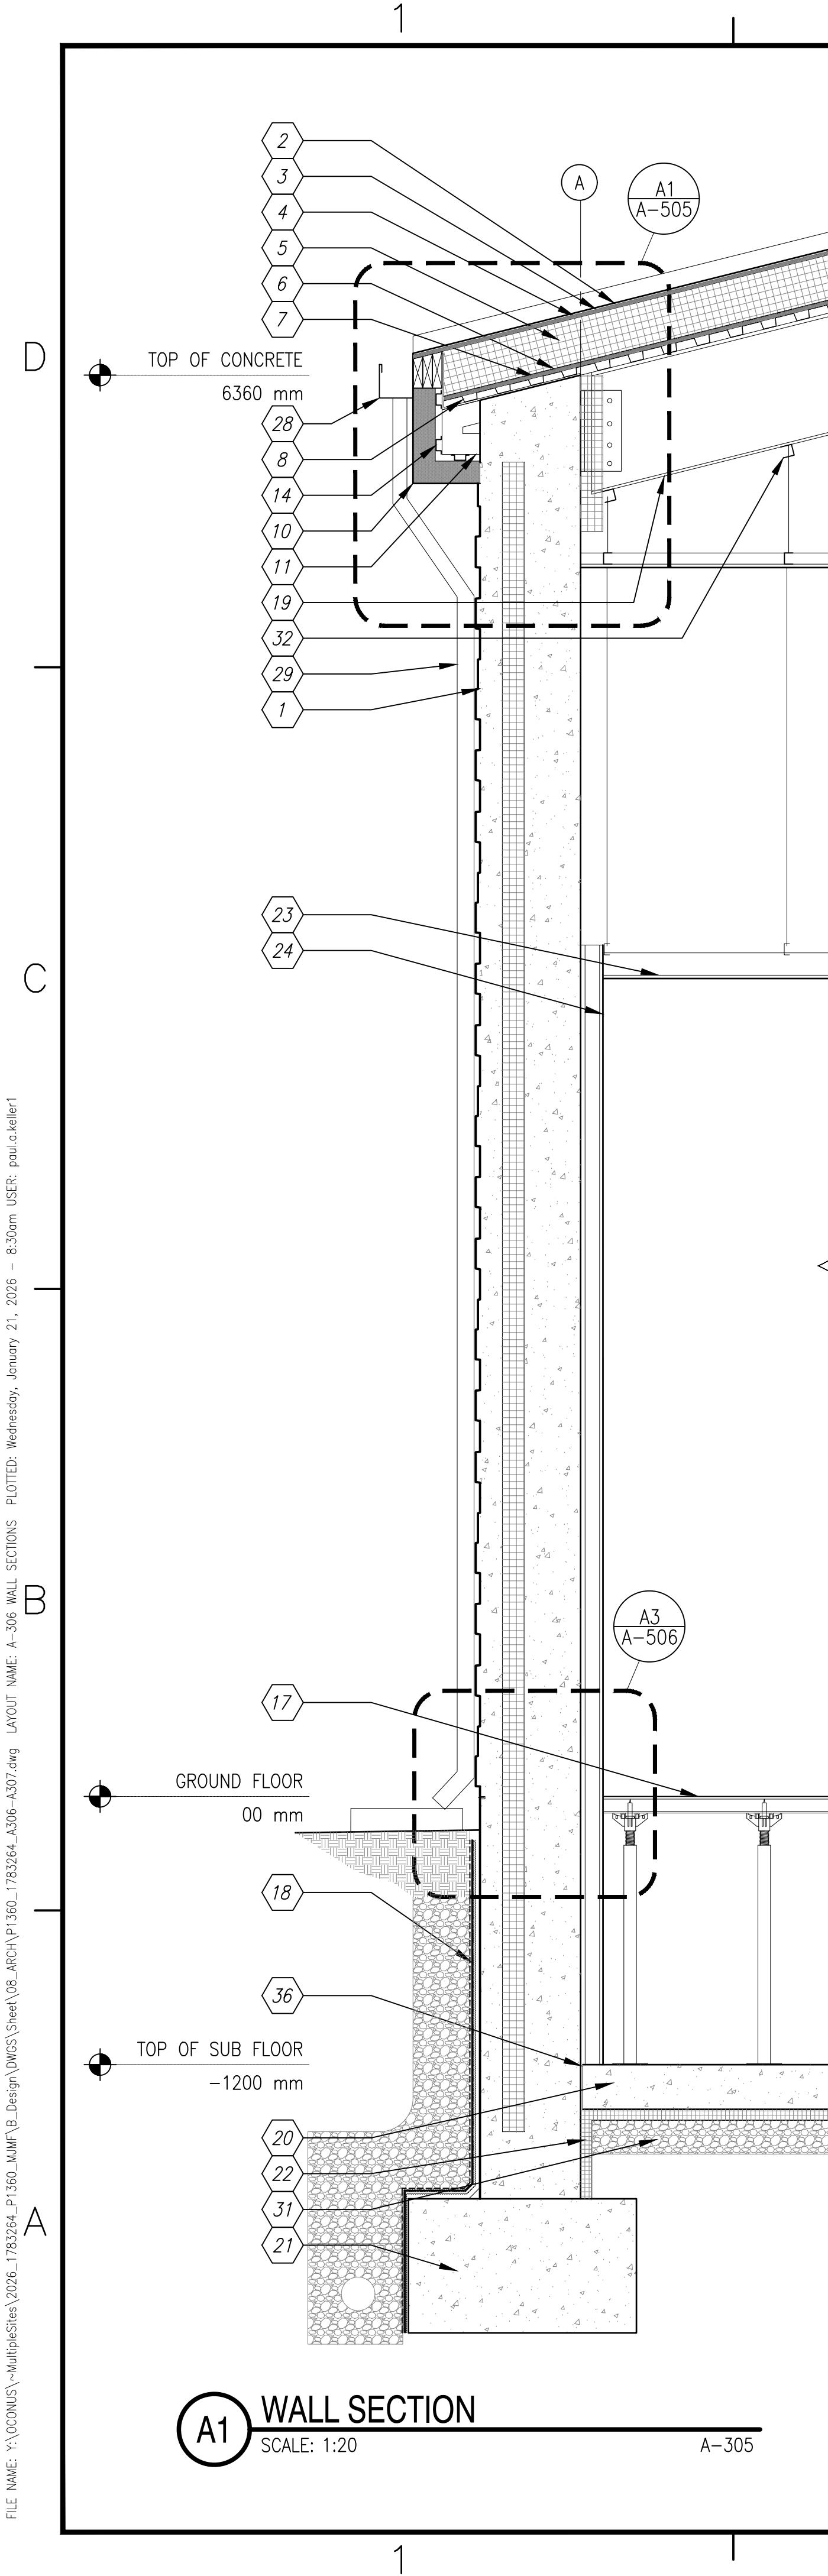


- ### GENERAL SHEET NOTES
- A. REFER TO SHEET A-001 FOR ARCHITECTURAL LEGEND AND ABBREVIATIONS.
 - B. REFER TO SHEET A-605 FOR PARTITION SCHEDULE.
 - C. REFER TO SHEET A-302 FOR KEYNOTES THIS SHEET.
 - D. SEE INTERIOR 'I' SERIES SHEETS FOR FINISH, FURNITURE AND EQUIPMENT LAYOUTS
 - E. PROVIDE FIRE RETARDANT TREATED WOOD BLOCKING FOR MOUNTING OF GRAB BARS, WALL MOUNTED CABINETS, AV OR IT EQUIPMENT, AND WHERE NECESSARY FOR PROPER ATTACHMENT OF ITEMS. SECURELY ATTACH BLOCKING TO METAL STUD FLANGES. COORDINATE EXACT LOCATION AND QUANTITY OF BLOCKING WITH EQUIPMENT REQUIRING REINFORCEMENT.
 - F. PROVIDE PLYWOOD BACKBOARDS WHERE REQUIRED FOR COMMUNICATIONS EQUIPMENT. ALL EXPOSED EDGES OF BACKBOARD SHALL BE PAINTED ON FIVE SIDES WITH A FIRE RETARDANT PAINT. SEE ELECTRICAL/TELECOM DRAWINGS FOR ADDITIONAL INFORMATION
 - G. FINISH FLOOR ELEVATION IS 0.00mm UNLESS OTHERWISE NOTED.



APPROVED
FOR COMMANDER NAVFAC
ACTIVITY
D. EVANS VIA EMAIL
SATISFACTORY TO DATE 01/15/2026
DES PAK DRW PAK JHR
PM/DM MJD/ATP
BRANCH MANAGER KMC
DES PROD DIR WBF
FIRE PROTECTION ENGINEER DSN

DEPARTMENT OF THE NAVY
NAVAL FACILITIES ENGINEERING SYSTEMS COMMAND
PLANNING, DESIGN AND CONSTRUCTION
NAVFAC
NAVFAC DRAWING NO. 14157129
SHEET 67 OF 170
A-306

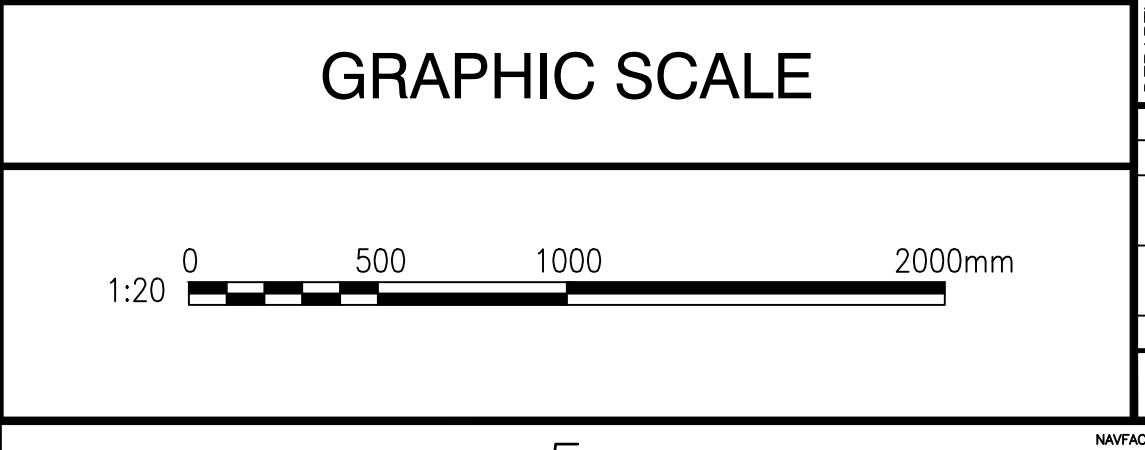





C

GENERAL SHEET NOTES

- A. REFER TO SHEET A-001 FOR ARCHITECTURAL LEGEND AND ABBREVIATIONS.
- B. REFER TO SHEET A-605 FOR PARTITION SCHEDULE.
- C. REFER TO SHEET A-302 FOR KEYNOTES THIS SHEET.
- D. SEE INTERIOR 'I' SERIES SHEETS FOR FINISH, FURNITURE AND EQUIPMENT LAYOUTS
- E. PROVIDE FIRE RETARDANT TREATED WOOD BLOCKING FOR MOUNTING OF GRAB BARS, WALL MOUNTED CABINETS, AV OR IT EQUIPMENT, AND WHERE NECESSARY FOR PROPER ATTACHMENT OF ITEMS. SECURELY ATTACH BLOCKING TO METAL STUD FLANGES. COORDINATE EXACT LOCATION AND QUANTITY OF BLOCKING WITH EQUIPMENT REQUIRING REINFORCEMENT.
- F. PROVIDE PLYWOOD BACKBOARDS WHERE REQUIRED FOR COMMUNICATIONS EQUIPMENT. ALL EXPOSED EDGES OF BACKBOARD SHALL BE PAINTED ON FIVE SIDES WITH A FIRE RETARDANT PAINT. SEE ELECTRICAL/TELECOM DRAWINGS FOR ADDITIONAL INFORMATION
- G. FINISH FLOOR ELEVATION IS 0.00mm UNLESS OTHERWISE NOTED.

- A. REFER TO SHEET A-001 FOR ARCHITECTURAL LEGEND AND ABBREVIATIONS.
- B. REFER TO SHEET A-605 FOR PARTITION SCHEDULE.
- C. REFER TO SHEET A-302 FOR KEYNOTES THIS SHEET.
- D. SEE INTERIOR 'I' SERIES SHEETS FOR FINISH, FURNITURE AND EQUIPMENT LAYOUTS
- E. PROVIDE FIRE RETARDANT TREATED WOOD BLOCKING FOR MOUNTING OF GRAB BARS, WALL MOUNTED CABINETS, AV OR IT EQUIPMENT, AND WHERE NECESSARY FOR PROPER ATTACHMENT OF ITEMS. SECURELY ATTACH BLOCKING TO METAL STUD FLANGES. COORDINATE EXACT LOCATION AND QUANTITY OF BLOCKING WITH EQUIPMENT REQUIRING REINFORCEMENT.
- F. PROVIDE PLYWOOD BACKBOARDS WHERE REQUIRED FOR COMMUNICATIONS EQUIPMENT. ALL EXPOSED EDGES OF BACKBOARD SHALL BE PAINTED ON FIVE SIDES WITH A FIRE RETARDANT PAINT. SEE ELECTRICAL/TELECOM DRAWINGS FOR ADDITIONAL INFORMATION
- G. FINISH FLOOR ELEVATION IS 0.00mm UNLESS OTHERWISE NOTED.

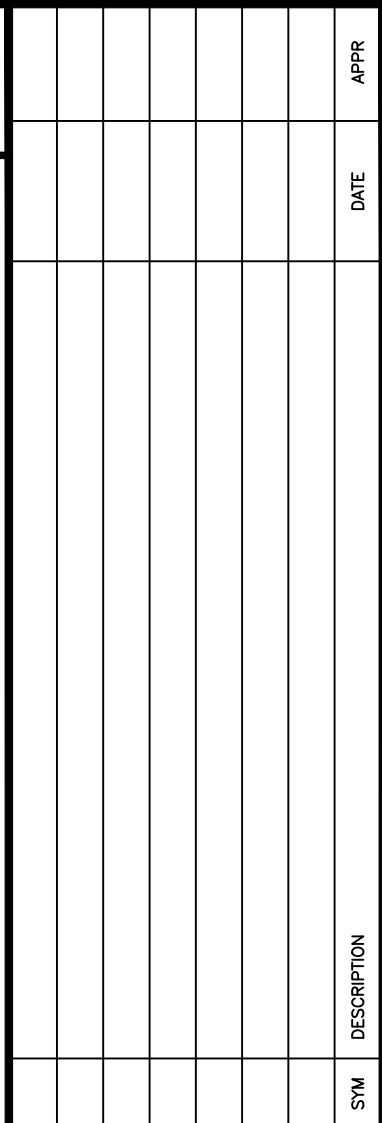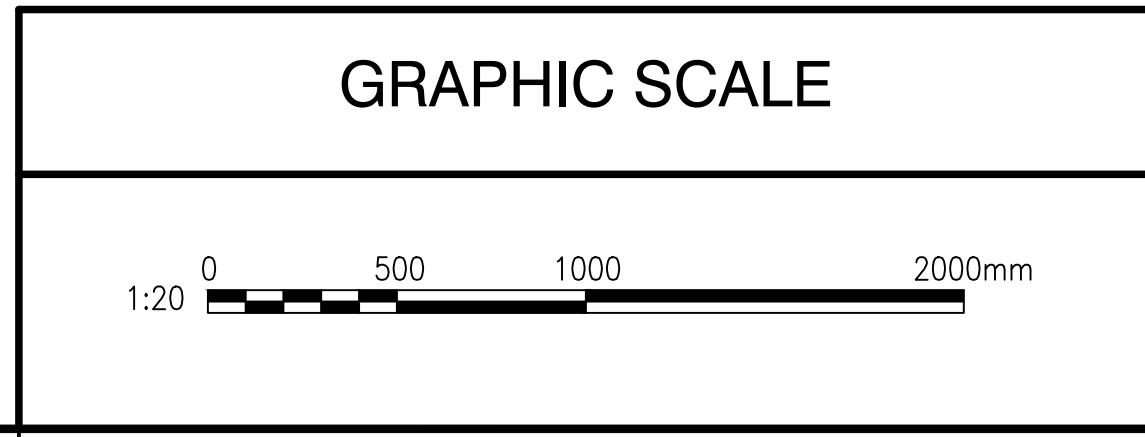[illegible][illegible][illegible]

1

2

3

4

5

KEYNOTES: ENLARGED PLANS AND INTERIOR ELEVATIONS

(FOR SHEETS A-405 AND A-406)

1

INTEGRAL SINK AND COUNTER. WALL MOUNTED WITH 100MM BACKSPLASH

2

TOILET. REFER TO PLUMBING DRAWINGS.

3

NON SLIP SOLID SURFACE SHOWER PAN, FULLY ADHERED TO SUBSTRATE. SLOPE FLOOR TO SIDE BELOW SHOWER SEAT. REFER TO INTERIOR DESIGN DRAWINGS.

4

SOLID SURFACE SHOWER WALL LINER. REFER TO INTERIOR DESIGN DRAWINGS.

5

ABA COMPLIANT FOLDING SHOWER SEAT. MUST COMPLY WITH D 293/2009

6

WALL CABINET, TYPICAL.

7

REFRIGERATOR. GFGI UNLESS OTHERWISE NOTED.

8

MICROWAVE. GFGI UNLESS OTHERWISE NOTED.

9

13mm THICK CONTINUOUS SOLID SURFACE BACKSPLASH TO FULL HEIGHT ABOVE HORIZONTAL SURFACE.

10

13mm THICK SOLID SURFACE COUNTERTOP OVER PLYWOOD SUBSTRATE.

11

MICROWAVE CABINET.

12

BASE PER SCHEDULE.

13

TOE KICK.

14

INTEGRAL SINK, REFER TO PLUMBING DRAWINGS.

15

DRAWER BASE, TYPICAL.

16

SINK BASE WITH INTEGRAL TOE KICK.

17

HAND HELD, ADJUSTABLE HEIGHT SHOWER HEAD WITH MIN 1800 MM LONG HOSE.

18

SHOWER CONTROL INSTALL AREA

19

ADA ACCESSIBLE HIGH/LOW WATER FOUNTAIN WITH BOTTLE FILLER. SEE PLUMBING DRAWINGS.

20

WALL TILE. REFER TO INTERIOR DESIGN DRAWINGS

21

STUD PARTITION REFER TO FLOOR PLAN AND PARTITION SCHEDULE.

22

SHOWER SETTING BED

23

CONCRETE SLAB, REFER TO STRUCTURAL

24

FLOOR FINISH, REFER TO INTERIOR DESIGN DRAWINGS.

25

SEALANT

26

PIPE PROTECTION

27

PAINTED DRYWALL

28

65MM LIGHT GAUGE METAL FRAMING

29

15MM GYPSUM WALL BOARD, PAINTED.

30

CORNER GUARD, REFER TO INTERIOR DRAWINGS.

31

STEEL COLUMN, REFER TO STRUCTURAL DRAWINGS

32

PRECAST CONCRETE WALL. REFER TO STRUCTURAL DRAWINGS.

33

JANITOR'S SINK. REFER TO PLUMBING DRAWINGS.

34

PRECAST CONCRETE CEILING BELOW, REFER TO STRUCTURAL DRAWINGS.

35

PRECAST CONCRETE WALL BELOW, REFER TO STRUCTURAL DRAWINGS.

36

100MM FABRICATED WALL PANEL ASSEMBLY AT SOFFIT BELOW WITH SMOOTH TEXTURE. MIN RSI-5.46

37

1HR SHAFTWALL ASSEMBLY PER UL U415. 25MM SHAFTLINER PANELS IN 100MM C-T STUDS WITH TWO LAYERS OF 15MM TYPE X GYPSUM WALLBOARD. PROVIDE 15MM FIRE CAULKING AT BASE AND JAMB PERIMETER OF TYPE X GYPSUM WALLBOARD. FILL WALL WITH MINERAL WOOL SOUND ATTENUATION BLANKETS. REFER FOR SHEET A-509 FOR ADDITIONAL INFORMATION.

38

T-9 STAINLESS STEEL SHELF

39

T-8 MOP AND BROOM HOLDER WITH SHELF, CENTERED OVER FLOOR SINK.

40

STAINLESS STEEL GRAB BARS

41

DOUBLE SIDE FOAM TAPE AT FULL PERIMETER OF SOLID SURFACE SHOWER WALL LINER PANELS.

42

CLEAR SILICONE SEALANT.

43

BASE CABINET, TYPICAL

44

JANITOR SINK AND FAUCET, REFER TO PLUMBING DRAWINGS.

45

FILLER PANEL TO MATCH CASEWORK.

46

STAINLESS STEEL UNDERMOUNT SINK, REFER TO PLUMBING DRAWINGS

47

SOLID PLASTIC LAMINATE FACED PHENOLIC CORE LOCKERS

KEYNOTES: CASEWORK

(FOR SHEET A-407)

1

CASEWORK WITH HIGH PRESSURE LAMINATE FINISH ON ALL EXPOSED SURFACES, TYPICAL.

2

PARTITION AS SCHEDULED.

3

ADJUSTABLE SHELF WITH STANDARDS, TYPICAL.

4

13mm THICK SOLID SURFACE COUNTERTOP OVER PLYWOOD SUBSTRATE.

5

EASED FRONT EDGE, TYPICAL.

6

DRAWER BASE, TYPICAL.

7

CONTINUOUS PERIMETER SEALANT.

8

WALL FINISH - REFER TO FINISH SCHEDULE

9

STAINLESS STEEL UNDERMOUNT SINK, REFER TO PLUMBING DRAWINGS

10

PLASTIC LAMINATE CABINET INTERIOR

11

13mm THICK CONTINUOUS SOLID SURFACE BACKSPLASH TO FULL HEIGHT ABOVE HORIZONTAL SURFACE.

12

BASE PER SCHEDULE.

13

DOOR/DRAWER PULL.

14

TOE KICK.

15

WALL CABINET, BEYOND.

16

PIPE PROTECTION

17

MICROWAVE-NOT IN CONTRACT.

18

MICROWAVE CABINET WITH HIGH PRESSURE LAMINATE FINISH ON ALL EXPOSED SURFACES.

19

CUTOUT FOR ACCESS TO ELECTRICAL OUTLET.

20

MIRROR.

21

WOOD BLOCKING, TYPICAL - PAINT TO MATCH WALL WHERE EXPOSED

22

FLOORING AS SCHEDULED

23

13MM THICK CONTINUOUS SOLID SURFACE BACKSPLASH TO 140MM ABOVE HORIZONTAL SURFACE

24

ALUMINUM COVE TRANSITION. SEE INTERIOR DRAWINGS.

25

CONCEALED COUNTERTOP SUPPORT BRACKETS. PROVIDE BLOCKING IN WALL AS REQUIRED FOR BRACKET ATTACHMENT. SET BACK TO ALLOW SHEATHING TO CONTINUE ACROSS BRACKET.

26

SOLID SURFACE SINK INTEGRAL WITH COUNTER, REFER TO PLUMBING DRAWINGS.

27

METAL FRAMED, FLOOR TO STRUCTURE ABOVE, BOX STUD TO MATCH WALL THICKNESS AND SCHEDULED WALL FRAMING. PROVIDE AT EACH LOCATION CONCEALED COUNTERTOP BRACKET IS LOCATED.



(



D1 **SHOWER PAN DETAIL**
SCALE: 1:10

B1 INTERIOR ELEVATION - ROOM 103
SCALE: 1:25

A1 INTERIOR ELEVATION - ROOM 105
SCALE: 1:25

B2 INTERIOR ELEVATION - ROOM 103
SCALE: 1:25

A2 INTERIOR ELEVATION - ROOM 102
SCALE: 1:25

TOILET ACCESSORIES SCHEDULE						
MARK ON DWGS	DESCRIPTION	MOUNTING	BASIS OF DESIGN			REMARKS
			MANUFACTURER	SERIES	MODEL NO.	
T-1	MIRROR WITH SS FRAME	SURFACE	BOBRICK		B-290	750 mm X 900 mm
T-1B	MIRROR WITH SS FRAME	SURFACE	ULINE		B-165 2460	24" X 60"
T-2	GRAB BAR	SURFACE	BOBRICK		B-68137.99	REFER TO ELEVATIONS FOR LENGTHS
T-3	SANITARY NAPKIN DISPOSAL	SURFACE	ULINE		H-3454	
T-4	PAPER TOWEL DISPENSER W/WASTE RECEPTACLE	RECESSED	BOBRICK		B-3944	C-FOLD TOWELS
T-5	TOILET TISSUE DISPENSER, MULTI-ROLL	SURFACE	BOBRICK		B-3588	
T-6	TOILET SEAT COVER DISPENSER	SURFACE	BOBRICK	CONTURA	B-4221	
T-7	SOAP DISPENSER (REFILLABLE)	SURFACE	SCOTT		MODEL 92145	4" X 8" X 5"
T-8	MOP AND BROOM HOLDER W/SHELF	SURFACE	BOBRICK		B-239 X 34	TOP OF SHELF AT 1800MM AFF
T-9	STAINLESS STEEL SHELF (CELL PHONE HOLDER)	SURFACE	BOBRICK		B-295 X 14	
T-10	TOWEL BAR	SURFACE	BOBRICK		B-6747 X 24	REFER TO ELEVATION AND DETAILS FOR LENGTHS
T-11	COAT HOOK	SURFACE	BOBRICK		B-549	
T-12	SHARPS CONTAINER	SURFACE	ULINE		S-24610	PROVIDE SHARPS CONTAINER INSERT

B3 INTERIOR ELEVATION - ROOM 104
SCALE: 1:25

B4 INTERIOR ELEVATION - ROOM 104
SCALE: 1:25

A5 INTERIOR ELEVATION - ROOM 106
SCALE: 1:25

A3 INTERIOR ELEVATION - ROOM 104
SCALE: 1:25

GENERAL SHEET NOTES

- A. REFER TO SHEET A-001 FOR ARCHITECTURAL LEGEND AND ABBREVIATIONS
- B. REFER TO SHEET A-401 FOR KEYNOTES THIS SHEET
- C. REFER TO 100 SERIES SHEETS FOR PARTITION AND CEILING TYPE LOCATIONS
- D. REFER TO INTERIOR DRAWINGS FOR WALL, FLOOR, CEILING, CASEWORK FINISH SELECTIONS




DEPARTMENT OF THE NAVY	NAVAL FACILITIES ENGINEERING SYSTEMS COMMAND
NAVAL FACILITIES ENGINEERING SYSTEMS COMMAND - ATLANTIC	
PLANNING, DESIGN AND CONSTRUCTION	NORFOLK, VA
VARIOUS LOCATIONS	VARIOUS LOCATIONS
JOINT MARITIME FACILITY	
INTERIOR ELEVATIONS AND TOILET ACCESSORIES SCHEDULE	


SCALE:	AS NOTED	
EPROJECT NO.:	1838720	
CONSTR. CONTR. NO.		
NAVFAC DRAWING NO.	14157133	
SHEET	71	OF 170
A-406		

NAVJAG METRIC DRAWFORM REVISION: 01 OCTOBER 20


FILE NAME: Y:\OCONUS\MultipleSites\2024_1783264_P1360_JAMFB_B_Design\DWG\Sheet\08_ARCH\VP1360_1783264_A406-A407.dwg LAYOUT NAME: A-407 CASEWORK SECTIONS PLOTTED: Wednesday, January 21, 2026 - 8:31am USER: paul.keller1

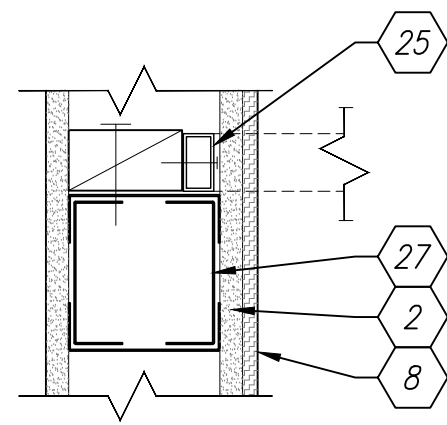


D1 PLANNED SECTION AT CONCEALED COUNTERTOP BRACKET
SCALE: 1:5 A-407

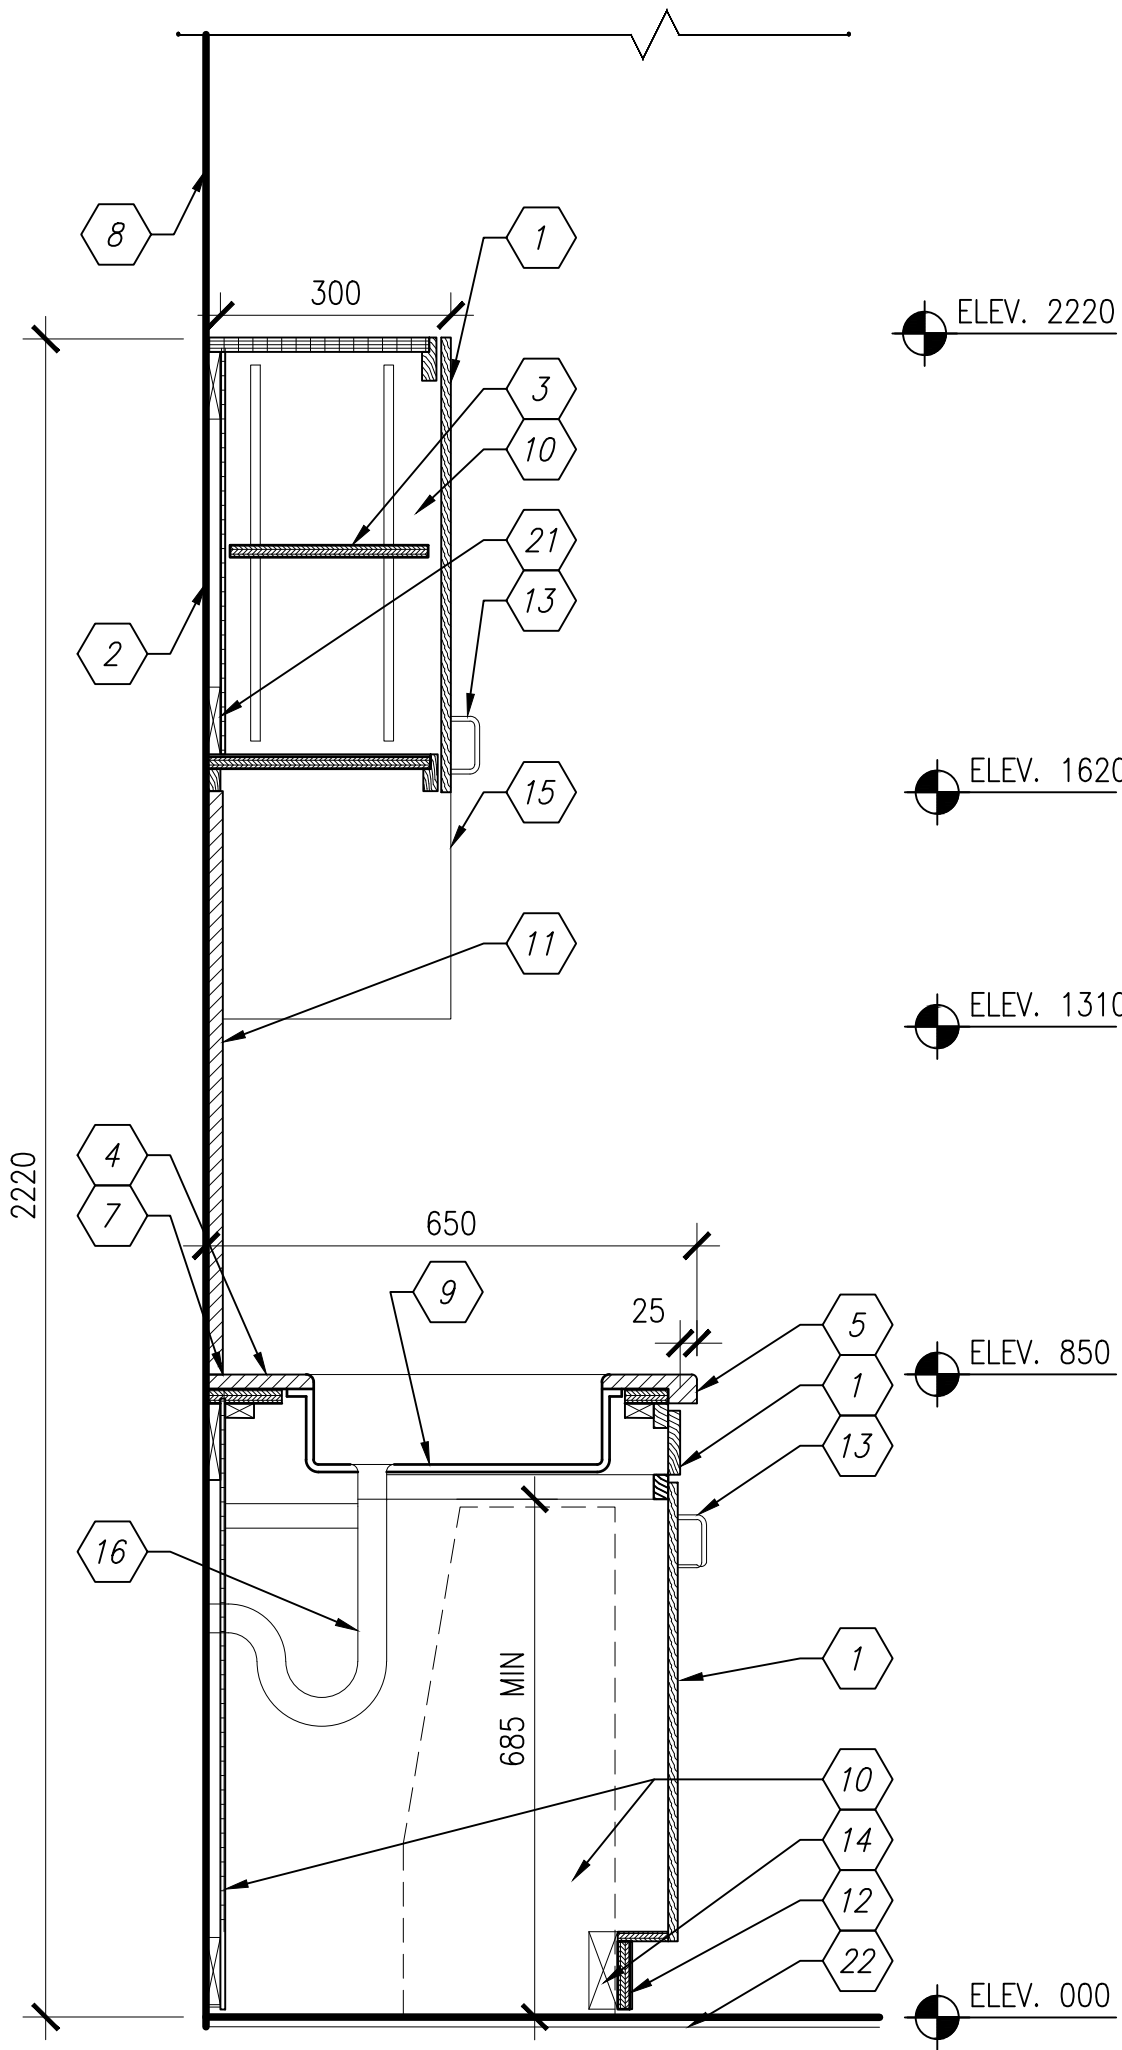


A1 SECTION AT CASEWORK - ROOM 105
SCALE: 1:10 A-406

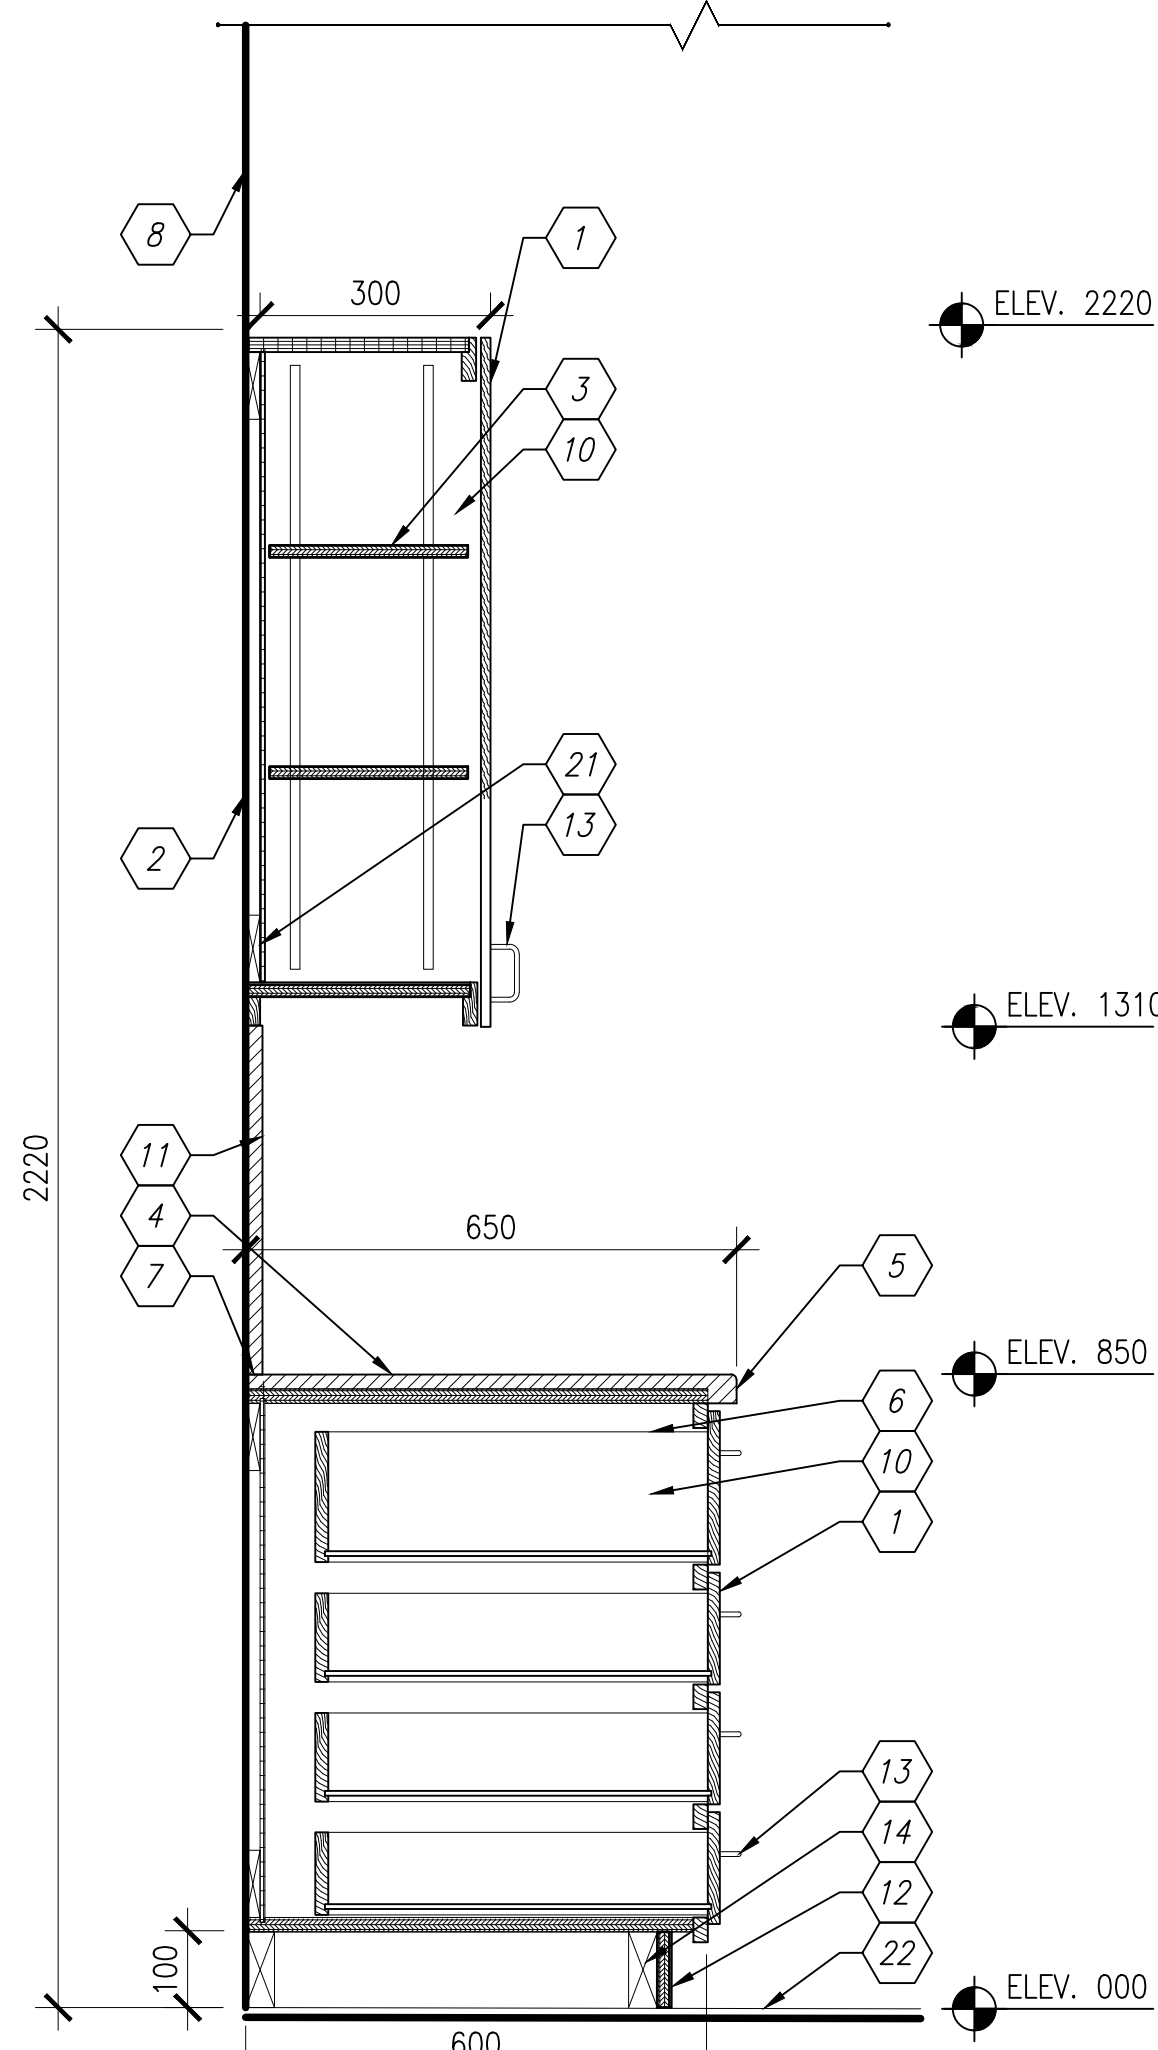

A2 SECTION AT CASEWORK - ROOM 105
SCALE: 1:10 A-406

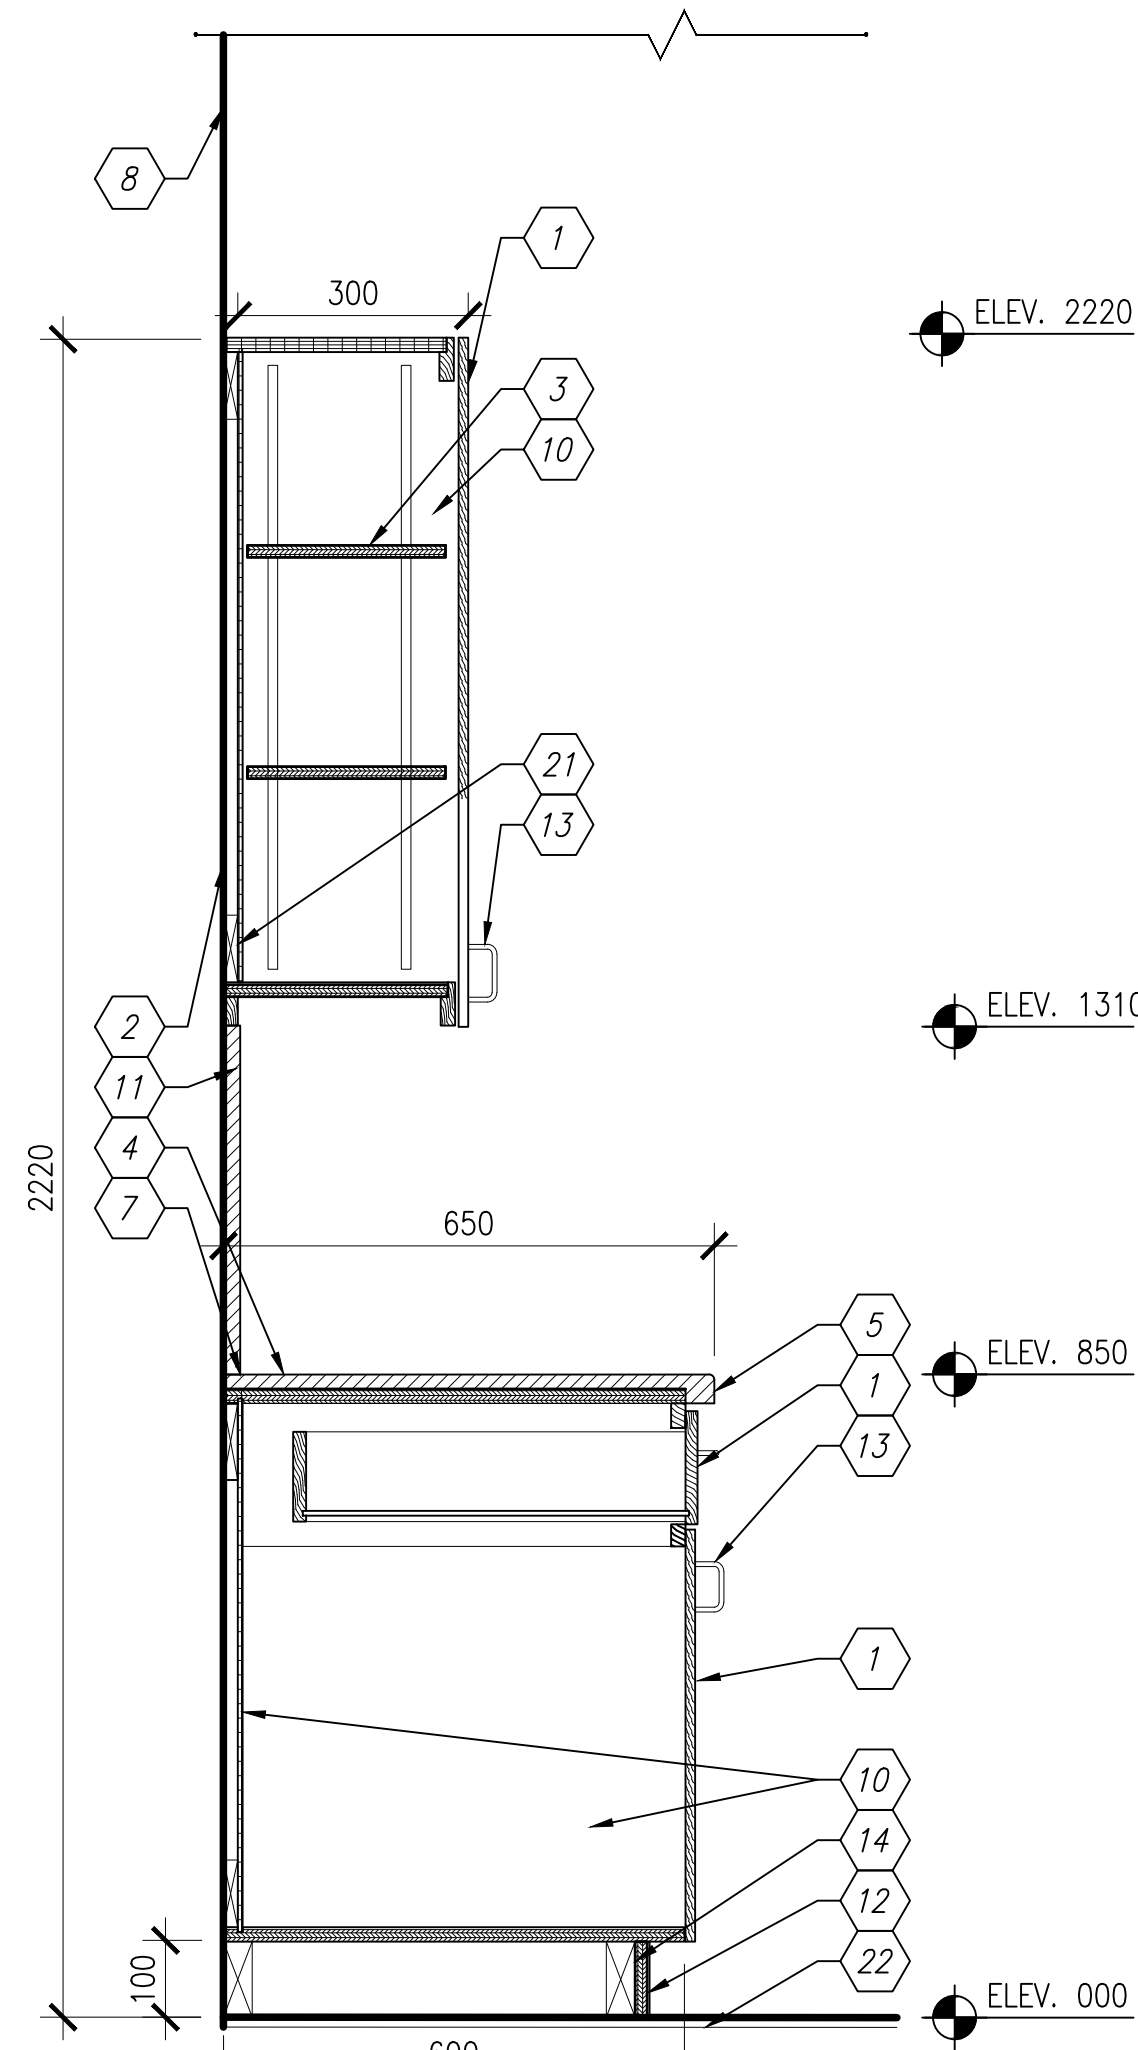

A3 SECTION AT CASEWORK - ROOM 105
SCALE: 1:10 A-406

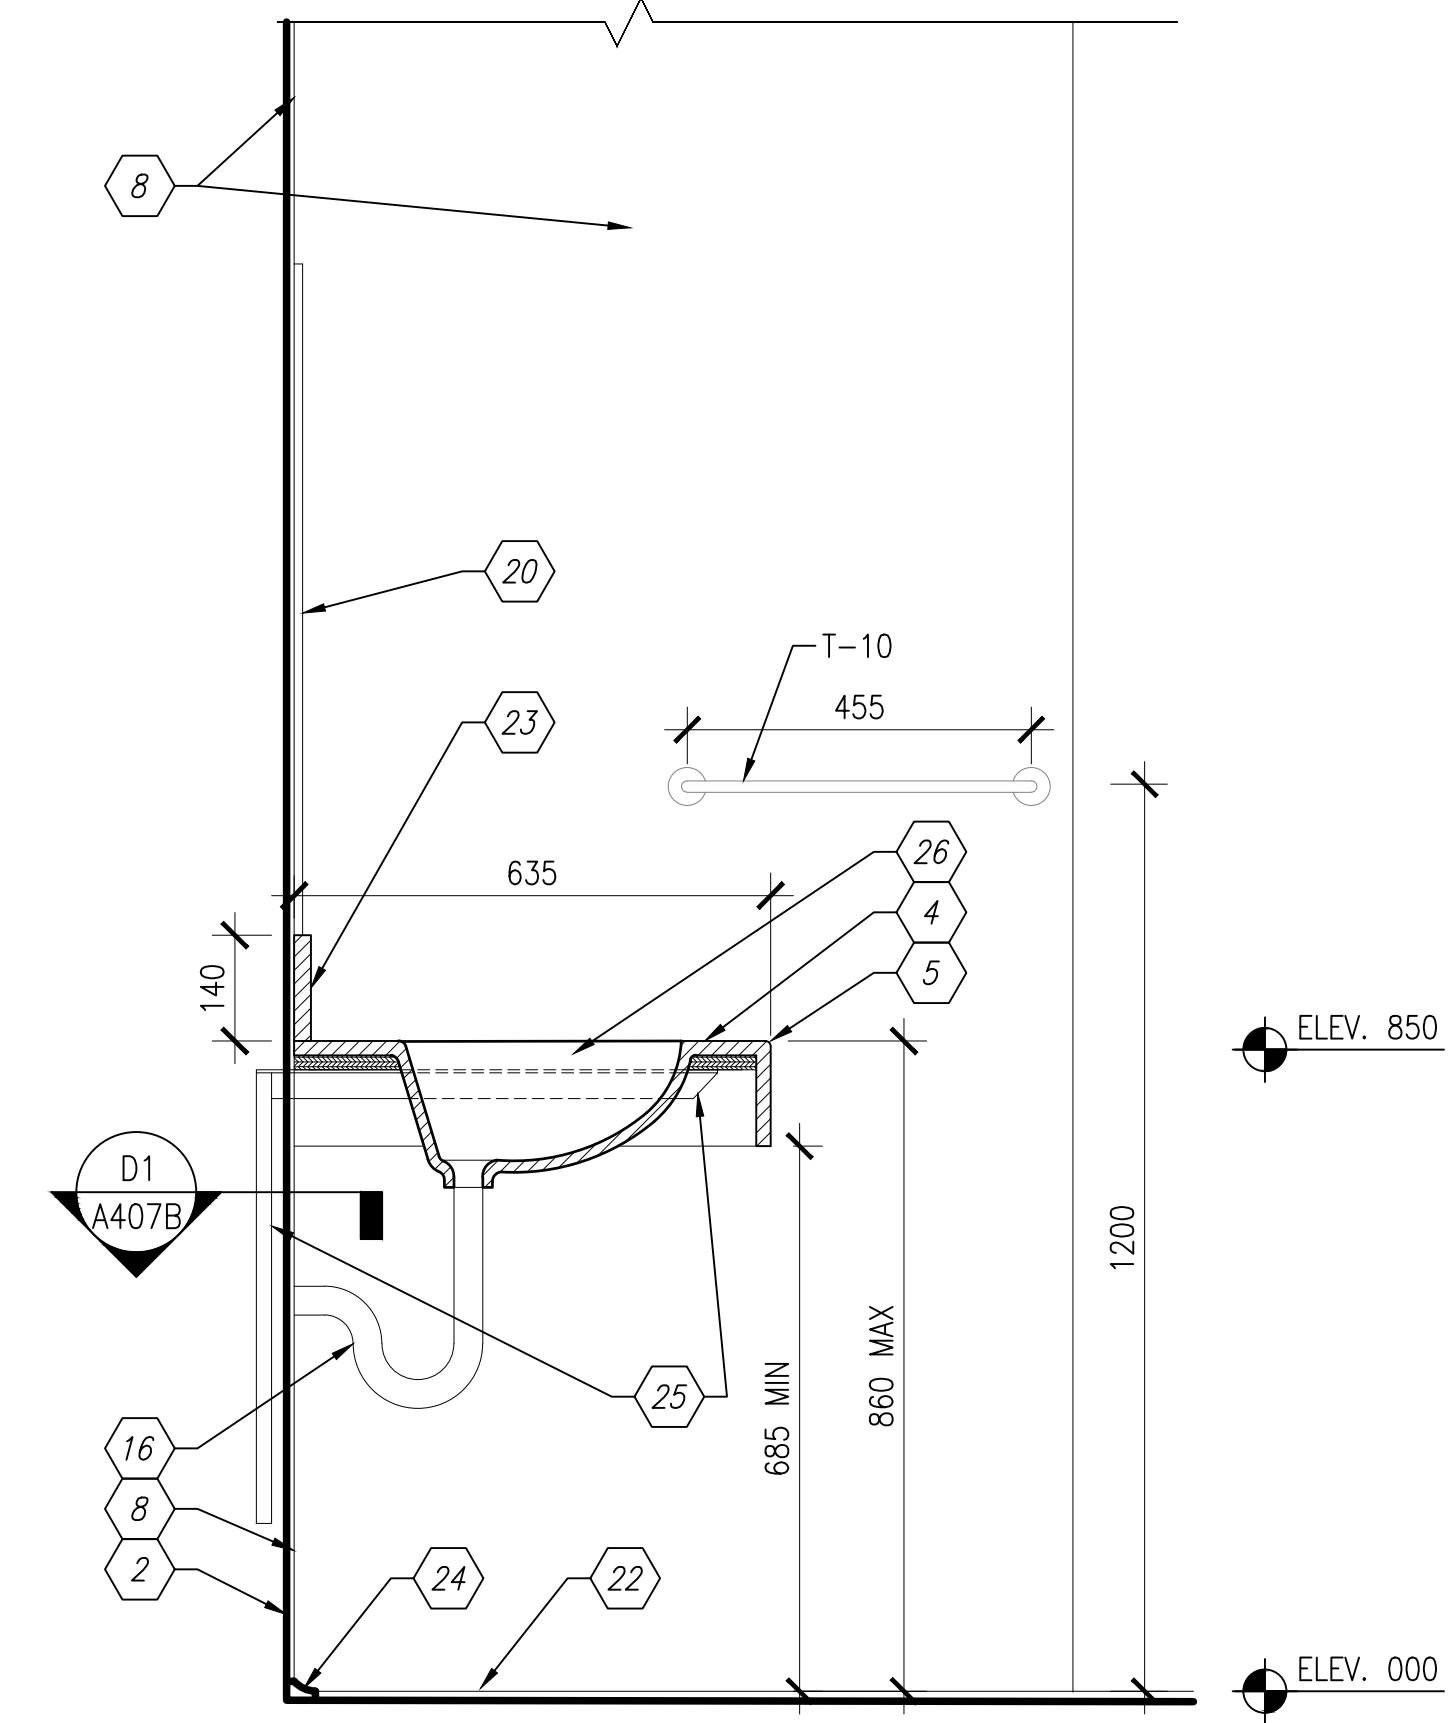

A4 SECTION AT CASEWORK - ROOM 104
SCALE: 1:10 A-406

GENERAL SHEET NOTES

- A. REFER TO SHEET A-001 FOR ARCHITECTURAL LEGEND AND ABBREVIATIONS
- B. REFER TO SHEET A-401 FOR KEYNOTES THIS SHEET
- C. REFER TO 100 SERIES SHEETS FOR PARTITION AND CEILING TYPE LOCATIONS



APPROVED

FOR COMMANDER NAVFAC

ACTIVITY

D. EVANS VIA EMAIL

SATISFACTORY TO DATE 01/15/2026

DES PAK DRW PAK

PM/DM MJD/ATP

BRANCH MANAGER KMC

DES PROD DIR WBF

FIRE PROTECTION ENGINEER DSN

NAVAL FACILITIES ENGINEERING SYSTEMS COMMAND

NAVAL FACILITIES ENGINEERING SYSTEMS COMMAND - ATLANTIC

NORFOLK VA

VARIOUS LOCATIONS

VARIOUS LOCATIONS

GRAPHIC SCALE

1:5 0 100 300 500mm

1:10 0 100 500 1000mm

SCALE: AS NOTED

APPROVED NO. 1838720

CONSTR. CONTR. NO.

NAVFAC DRAWING NO.

14157134

SHEET 72 OF 170

A-407

NAVFAC METRIC DRAWING REVISION: 01 OCTOBER 2018

1

2

3

4

5

WORK KEYNOTES - EXTERIOR DETAILS

(FOR SHEETS A-505 TO A-506)

1

PRE-FINISHED ALUMINUM CONDUCTOR HEAD

2

SCUPPER BEYOND

3

OVERFLOW SCUPPER BEYOND

4

PROVIDE 100mm x 100mm OVERFLOW OPENING @ SIDE OF CONDUCTOR HEAD

5

LEADERBOX DIVIDER BEYOND

6

125mm WIDE x 125mm DEEP SQUARE PRE-FINISHED ALUMINUM DOWNSPOUT

7

THRU-WALL SHEET METAL FLASHING

8

CONTINUOUS SEALANT – TOOL TO FACILITATE WATER RUNOFF WHERE REQUIRED.

9

0.5mm THICK STAINLESS STEEL FACE PLATE

10

STAINLESS STEEL SCUPPER INSERT. ADHERE TO DECK AND PARAPET WALL WITH COMPATIBLE ROOF CEMENT – PRIME FLANGE

11

WRAP OPENING WITH SELF-ADHERING FLASHING / VAPOR IMPERMEABLE AIR BARRIER SYSTEM.

12

GALVANIZED METAL ROOF DECKING – SEE STRUCTURAL DWGS

13

PRECAST CONCRETE – SEE STRUCTURAL DRAWINGS

14

CONTINUOUS 200mm THICK RIGID POLYSOCYANURATE ROOF INSULATION BOARDS (RSI-6.93 MIN). PROVIDE TWO LAYERS OF 100MM BOARDS WITH STAGGERED JOINTS.

15

15.875MM (5/8 IN) TYPE X GLASS MAT GYPSUM ROOF COVER BOARD

16

MODIFIED BITUMEN ROOF ASPHALT SMOOTH BASE SHEET

17

MODIFIED BITUMEN ROOF SMOOTH PLY SHEET

18

MODIFIED BITUMEN ROOF CAP SHEET – PREP SURFACE FOR FLASHING

19

MODIFIED BITUMEN ROOF BACKER SHEET WITH SEALED LAPS.

20

MODIFIED BITUMEN ROOF FLASHING SHEET – FULLY ADHERE TO TOP PLY SHEET AND CAP SHEET

21

100mm CONTINUOUS RIGID INSULATION CANT STRIP

22

VENT PIPING – SEE PLUMBING DRAWINGS

23

PRE-FINISHED WIND CLIP – FASTEN TO WALL @ 600mm O/C MAX

24

PRE-FINISHED METAL RECEIVER WITH REMOVABLE PRE-FINISHED COUNTERFLASHING. FASTEN COUNTERFLASHING @ 150mm O/C MAX

25

ELASTOMERIC COATING OVER 15.875MM (5/8 IN) TYPE X GYPSUM ROOF COVER BOARD

26

SELF-ADHERING TRANSITION FLASHING

27

CONTINUOUS 100mm RIGID EXTRUDED POLYSTYRENE (XPS) WALL INSULATION BOARD. RSI-3.64 MIN.

28

CONTINUOUS SEALANT AND BACKER ROD

29

TAPERED INSULATION ROOF CRICKET

30

MODIFIED BITUMEN FLASHING – OVERLAP ROOFING SHEET MIN. 100mm. EXTEND MIN. 100mm ABOVE EDGE OF ROOFING SHEET.

31

60MM TRIPLE LOCKED MECHANICALLY SEAM PRE-FINISHED STANDING SEAM METAL ROOF. PROVIDE SEALANT IN ALL SEAMS.

32

100MM THICK FABRICATED WALL PANEL ASSEMBLY. EMBOSSED TEXTURE. RSI 3.64.

33

STANDOFF CLIP BY STANDING SEAM ROOF MANUFACTURER. FASTEN INTO BEARING PLATE AT EACH CLIP.

34

EAVE TRIM BY STANDING SEAM ROOF MANUFACTURER.

35

GABLE TRIM CAP, BY STANDING SEAM ROOF MANUFACTURER

36

GABLE TRIM STARTER CLEAT, BY STANDING SEAM ROOF MANUFACTURER

37

RIDGE CAP, BY STANDING SEAM ROOF MANUFACTURER

38

NEOPRENE, BY STANDING SEAM ROOF MANUFACTURER

39

150MM X 150MM HEAVY GAUGE BEARING PLATE (BY STANDING SEAM ROOF MANUFACTURER) AT EACH STANDOFF CLIP ON TOP OF UNDERLAYMENT. FASTEN THROUGH RIGID INSULATION TO ROOF DECK BELOW WITH MIN TWO FASTENERS.

40

50MM RIGID MINERAL WOOL INSULATION

41

SELF ADHERING HIGH TEMPERATURE ICE & WATER SHIELD. 915MM WIDE (MIN) AT BASE OF ROOF SLOPE AND ROOF EDGE ALONG RAKE AND EAVE. LAP DOWN AND OVER EAVE/RAKE TRIM, 50 MM MIN WHERE APPLICABLE.

42

SELF-ADHERING MEMBRANE FLASHING. LAP OVER ROOF SHEATHING AND CONTINUE DOWN OVER PRESSURE TREATED BLOCKING AND FABRICATED WALL PANELS, 50 MM MIN. ASSURE FLASHING IS CONCEALED BEHIND METAL TRIM AND GUTTER.

43

Z CLOSURE, BY STANDING SEAM ROOF MANUFACTURER

44

30MM HAT CHANNELS, 16GA MIN

45

150mm x 150mm PRE-FINISHED ALUMINUM GUTTER

46

LINER FLASHING BY FABRICATED WALL PANEL MANUFACTURER

47

CLIP AND FASTENER BY FABRICATED WALL PANEL MANUFACTURER.

48

PANEL END FLASHING BY FABRICATED WALL PANEL MANUFACTURER

49

TWO PIECE SOFFIT FLASHING BY FABRICATED WALL PANEL MANUFACTURER. CONTINUE UP BEHIND FABRICATED WALL PANEL SYSTEM BEYOND WALL FASTENER.

50

SOFFIT TRIM BY FABRICATED WALL PANEL MANUFACTURER.

51

STEEL ANGLE OUTRIGGER, REFER TO STRUCTURAL DRAWINGS.

52

OUTSIDE/INSIDE CORNER FLASHING BY FABRICATED WALL PANEL MANUFACTURER.

53

PRESERVATION TREATED WOOD BLOCKING

54

PREFINISHED METAL COPING

55

100MM RIGID MINERAL WOOL INSULATION

56

SELF ADHERED AIR BARRIER

57

STEEL BEAM, REFER TO STRUCTURAL DRAWINGS

58

STEEL ANGLE, REFER TO STRUCTURAL DRAWINGS

59

PRECAST COPING BELOW

60

SUSPENDED GYPSUM WALL BOARD CEILING ASSEMBLY

61

CONTINUOUS DEEP LEG, COLD FORMED STEEL, DEFLECTION TRACK TO RECEIVE METAL STUDS. FILL FLUTES IN METAL DECK ABOVE CHANNEL WITH FIRESTOPPING MATERIAL TO MATCH PARTITION RATING. REFER TO PARTITION SCHEDULE FOR TYPE.

62

STEEL LADDER:
– 65MM X 8MM STEEL LADDER SIDE STRINGER – PAINT.
– 20MM DIAMETER RUNGS AT 300MM O/C. – PAINT

63

STEEL STAND-OFF ANGLE WELDED TO STRINGER AND SECURED TO HEAVY GAUGE BOX STUDS IN WALL. SUPPORTS BY LADDER MANUFACTURER. SPACING PER MANUFACTURER RECOMMENDATIONS.

64

INSULATED ROOF ACCESS HATCH (1200MM X 1200MM) AND SELF-CLOSING/LATCHING GUARD RAIL AND GATE SYSTEM BY SAME MANUFACTURER. PROVIDE INTEGRAL CLIP SYSTEM TO TERMINATE ROOFING MEMBRANE.

65

BENT PLATE, 16 GA MIN

66

STEEL OPENING SUPPORT, REFER TO STRUCTURAL DRAWINGS.

67

EXTENDABLE SAFETY POST FROM LADDER ASSEMBLY. EXTEND ONE METER MINIMUM.

68

INTERIOR WALL AS SCHEDULED

69

PRE-FINISHED METAL FLANGE SET IN COMPATIBLE ROOF CEMENT – PRIME BEFORE STRIPPING

70

VANDAL-PROOF VENT CAP

71

CONTINUOUS SELF ADHERING SEALANT TAPE

72

STAINLESS STEEL DRAWBAND

73

STAINLESS STEEL UMBRELLA RAIL COUNTER FLASHING

74

COMPRESSIBLE MINERAL WOOL INSULATION

75

CONTINUOUS WATERPROOFING APPLIED TO BELOW GRADE FACE OF PRECAST CONCRETE PANELS. AT BUILDING EXTERIOR LOCATIONS, TERMINATE 50MM BELOW GRADE WITH TERMINATION BAR AND SEALANT BY WATERPROOFING MANUFACTURER. AT SUB-FLOOR BUILDING INTERIOR LOCATIONS TERMINATE 20MM BELOW FINISH FLOOR ELEVATION, AND SEAL JOINT WITH BACKERROD AND SEALANT BY WATERPROOFING MANUFACTURER. EXTEND OVER TOP OF AND DOWN FACE OF FOOTER. PROVIDE INTEGRAL WATERPROOF TRANSITION FLASHING AT CONCRETE JOINTS, BY WATERPROOFING MANUFACTURER. PROTECTION PROTECTION BOARD OVER EXTENTS OF WATER PROOFING. PROVIDE COMPATIBLE DRAINAGE MAT BY WATERPROOFING MANUFACTURER ON EXTERIOR FACE OF ASSEMBLY.

76

BOTTOM EXTENTS OF PRECAST CONCRETE FORMLINER TEXTURE TO ALIGN WITH FINISHED FLOOR, 0.0

77

GRADE, REFER TO CIVIL DRAWINGS.

78

RAISED ACCESS FLOORING, REFER TO INTERIOR DRAWINGS

79

FIRE CAULK TO FULL DEPTH OF WALL MATERIAL PER UL HW-D-0908

80

FILL FLUTES OF METAL DECK ABOVE WALL WITH FIRESTOPPING MATERIAL.

APPROVED

FOR COMMANDER NAVFAC

ACTIVITY

D. EVANS VIA EMAIL

SATISFACTORY TO: DATE: 01/15/2026

DWG: PAK DRW PAK CHG JHR

PN/OW MJD/ATP

BRANCH MANAGER KMC

DWG PROD DIR WBF

FIRE PROTECTION ENGINEER DSN

DEPARTMENT OF THE NAVY

NAVAL FACILITIES ENGINEERING SYSTEMS COMMAND

NAVAL FACILITIES ENGINEERING SYSTEMS COMMAND - ATLANTIC

PLANNING, DESIGN AND CONSTRUCTION

VARIOUS LOCATIONS

VARIOUS LOCATIONS

VARIOUS LOCATIONS

JOINT MARITIME FACILITY

WORK KEYNOTES – EXTERIOR DETAILS

SCALE: AS NOTED

EPROJECT NO.: 1838720

CONSTR. CONTR. NO.

NAVFAC DRAWING NO. 14157135

SHEET 73 OF 170

A-501

1

2

3

4


5

FILE NAME: Y:\CONUS\MultipleSheets\2026_1783264_P1360_MJM\B.Design\DWGS\Sheet\08_ARCH\VT1360_1783264_A501.dwg

LAYOUT NAME: A-501 WORK KEYNOTES EXTERIOR DETAILS PLOTTED: Wednesday, January 21, 2026 – 8:31am USER: paula.keller1

A


FILE NAME: Y:\OCONUS\MultiPhase\2024_1783264_P1362_JMMP\B_Design\DWG\Sheet\08_ARCH\PT1362_1783264_A505-A506.dwg LAYOUT NAME: A-505 ROOF DETAILS PLOTTED: Wednesday, January 21, 2026 - 8:31am USER: paul.keller1

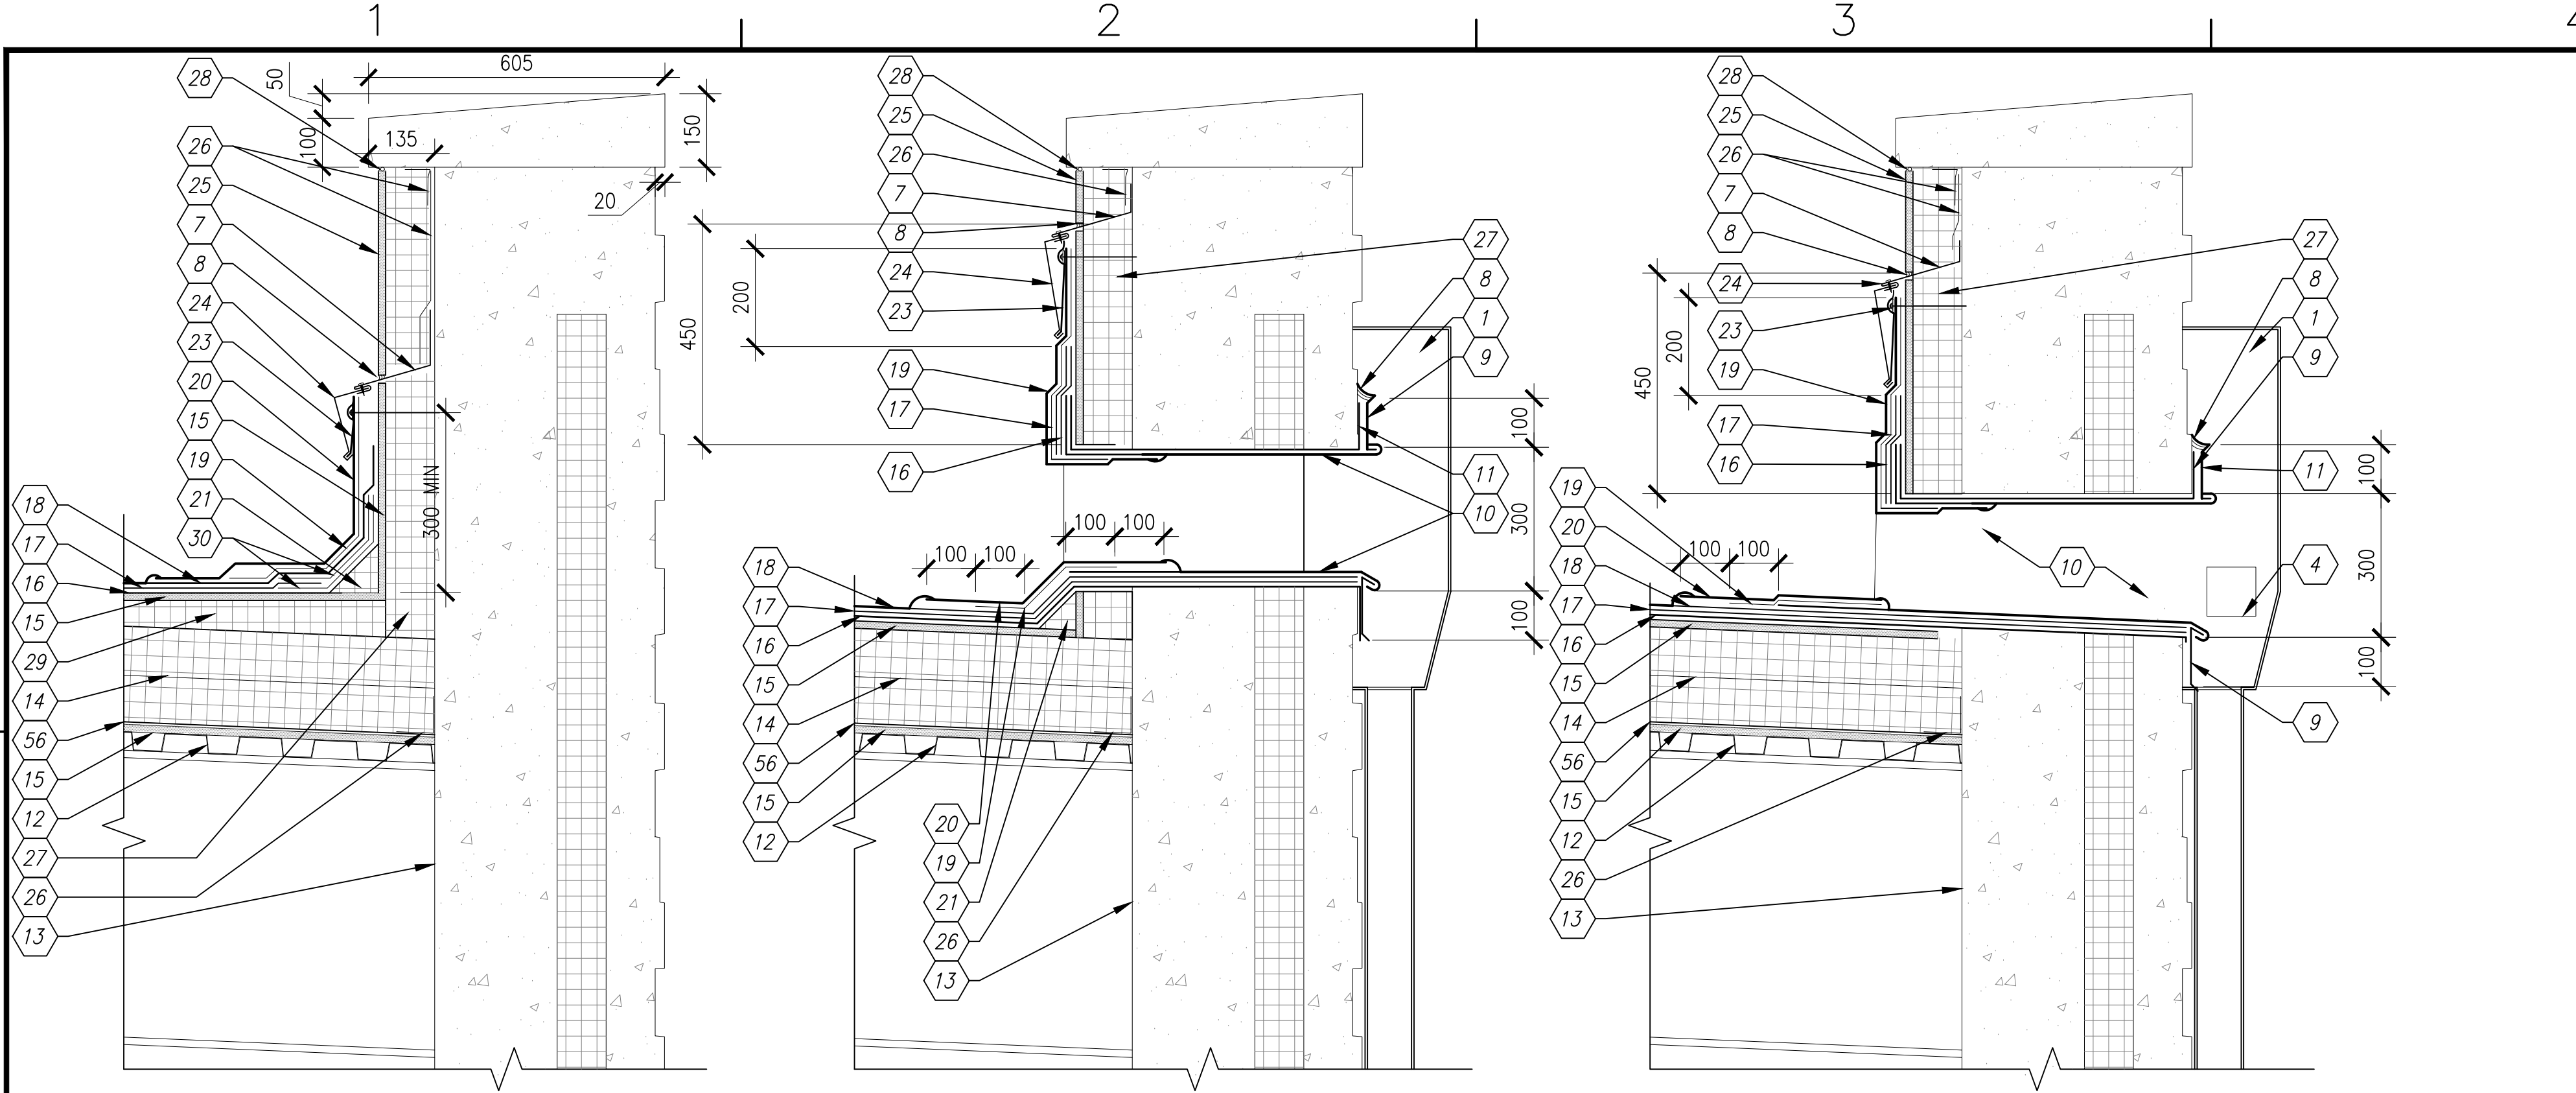

C1 PARAPET DETAIL
SCALE: 1:10
A-306


C2 OVERFLOW SCUPPER DETAIL
SCALE: 1:10
A-107, A-506

C3 SCUPPER DETAIL
SCALE: 1:10
A-107, A-506

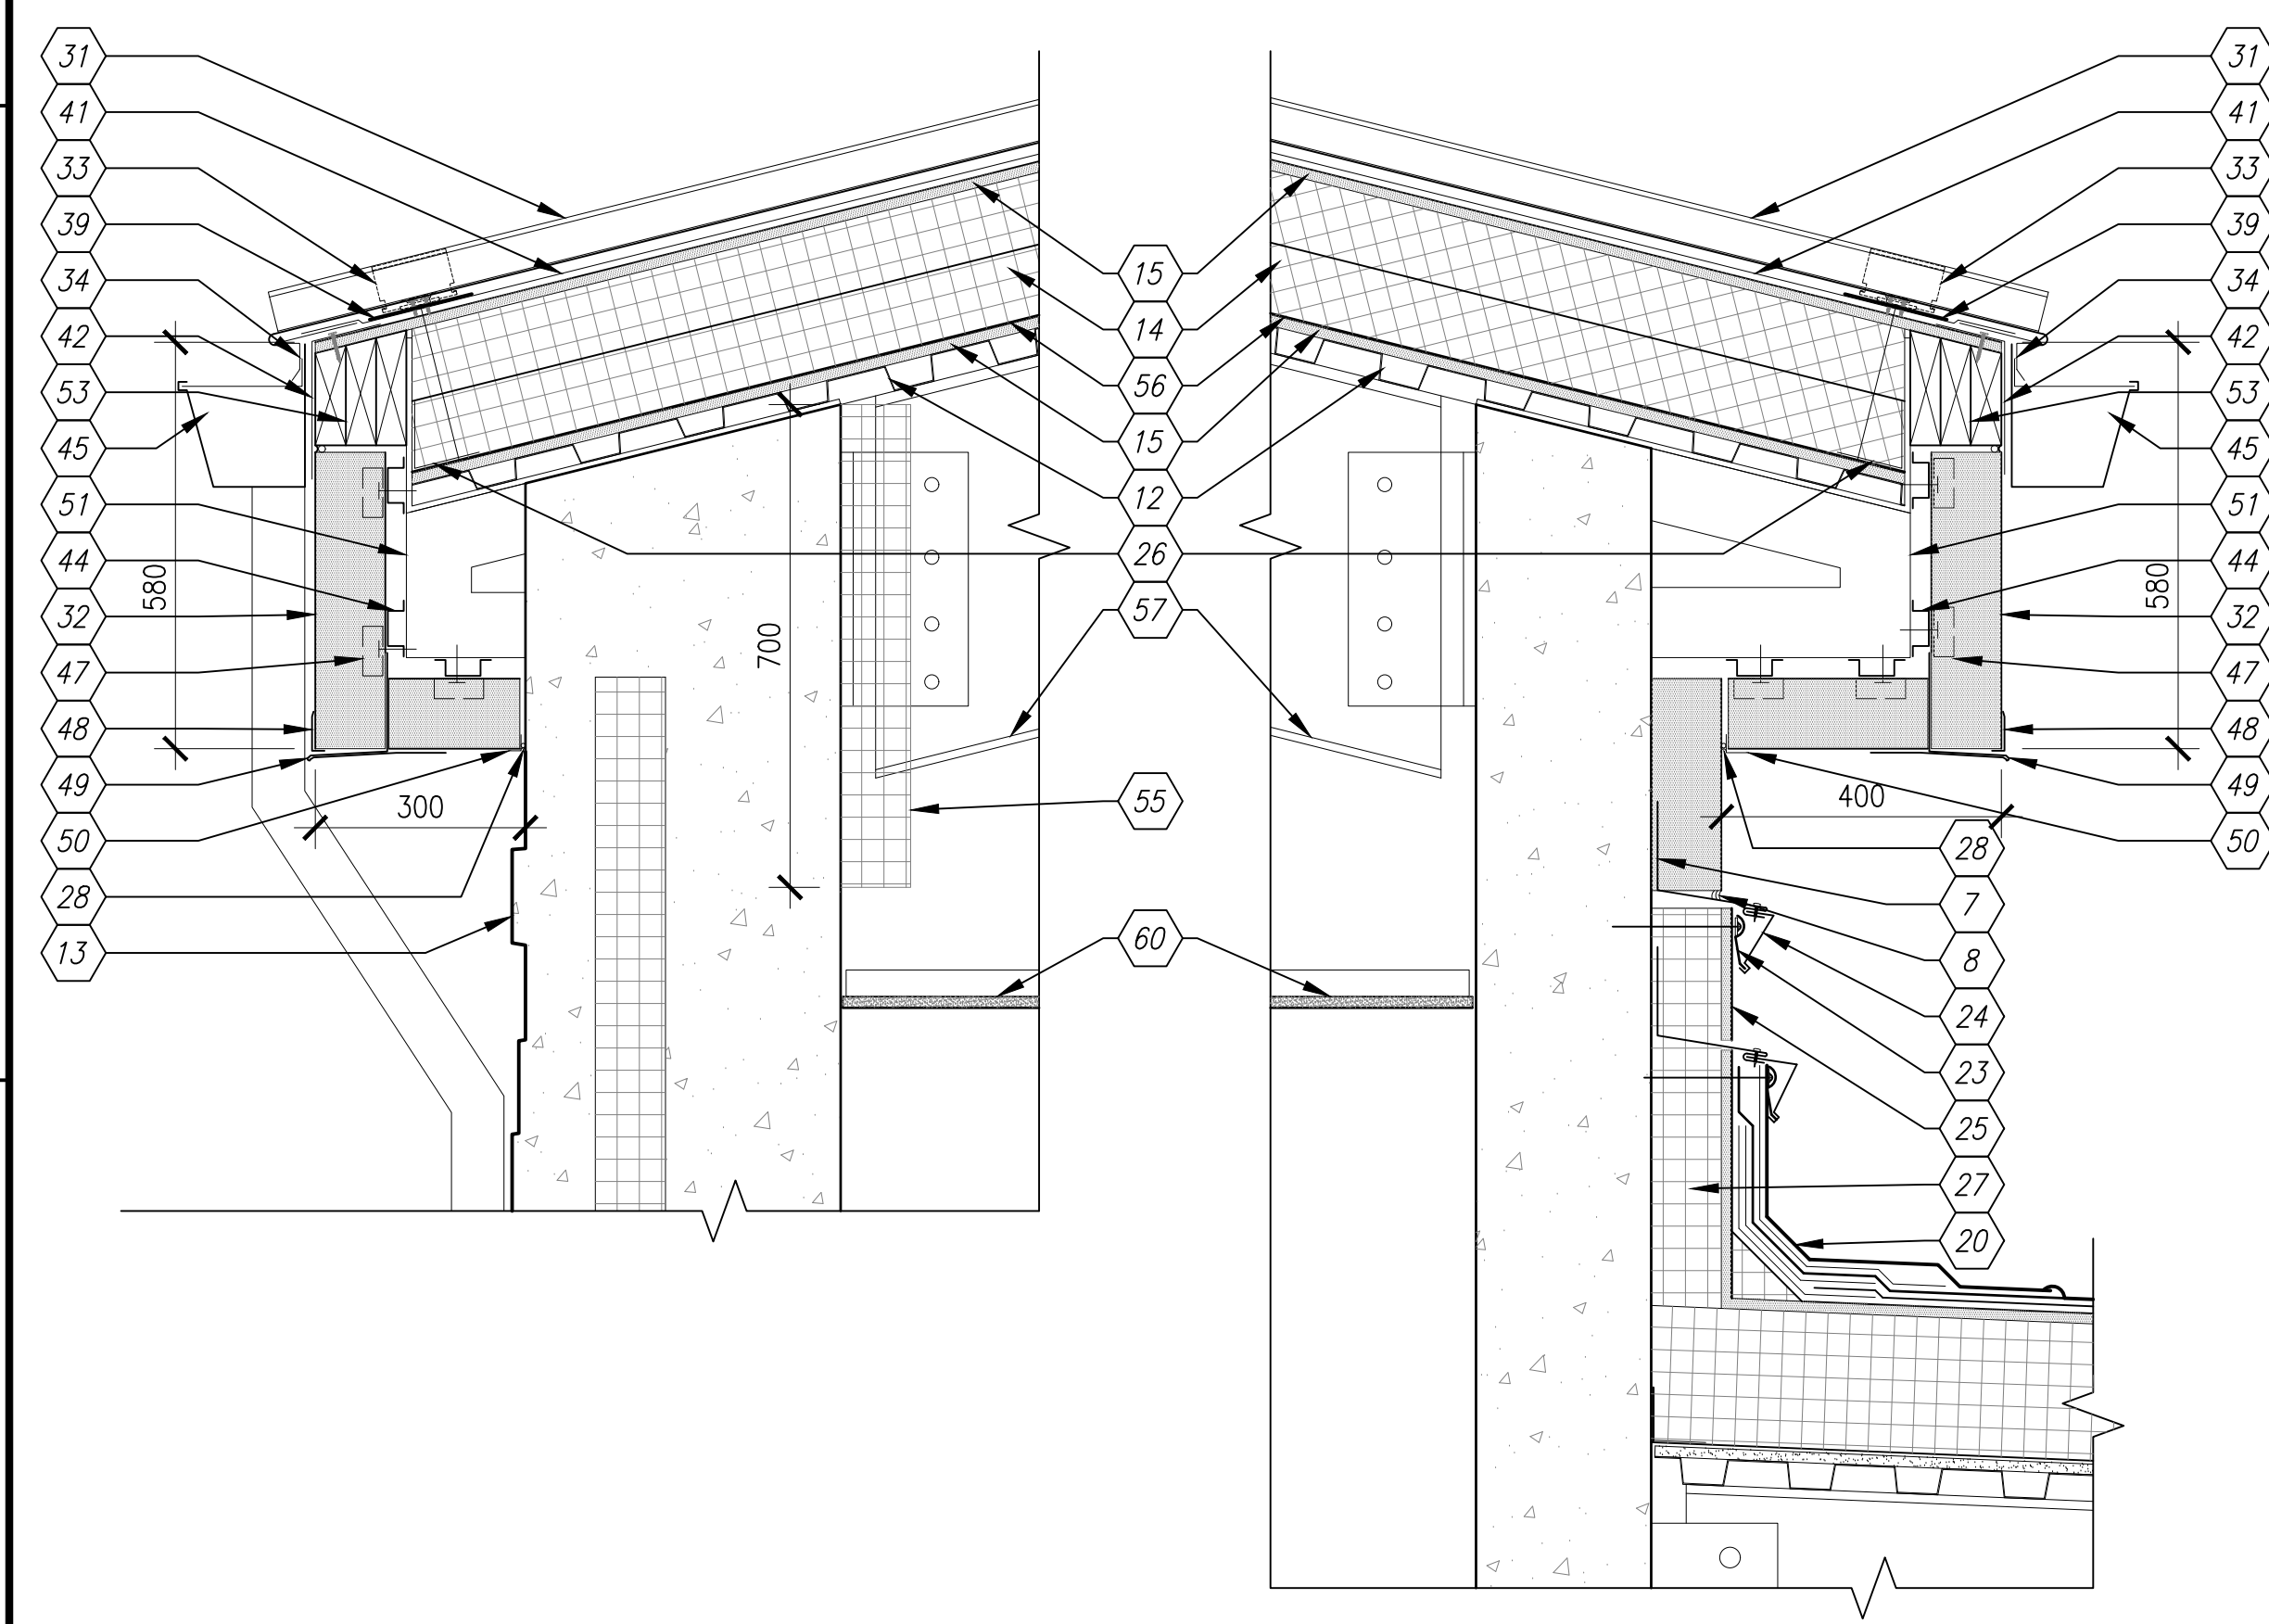


A1 HIGH ROOF EAVE DETAIL
SCALE: 1:10
A-306


A2 HIGH ROOF EAVE DETAIL
SCALE: 1:10
A-306

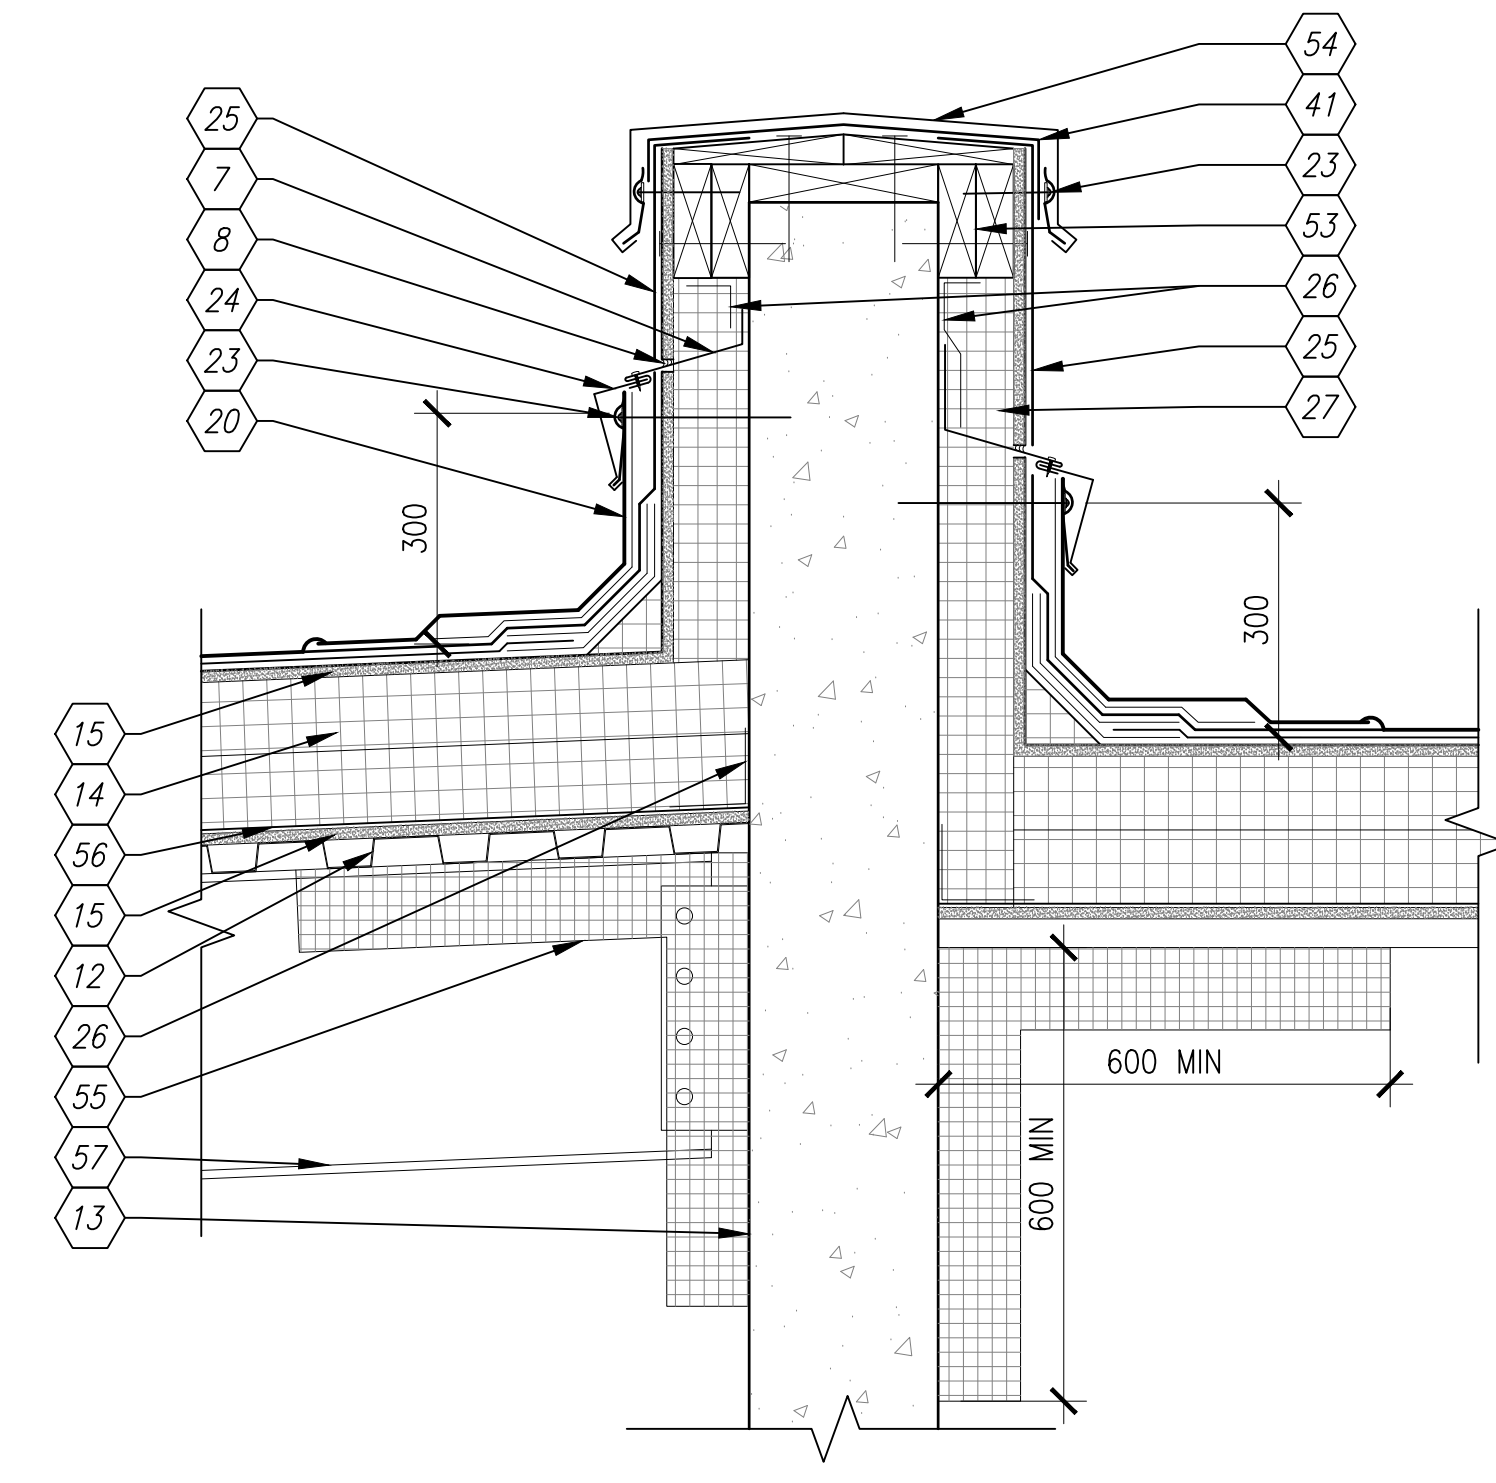

A3 ROOF CURB DETAIL
SCALE: 1:10
A-107

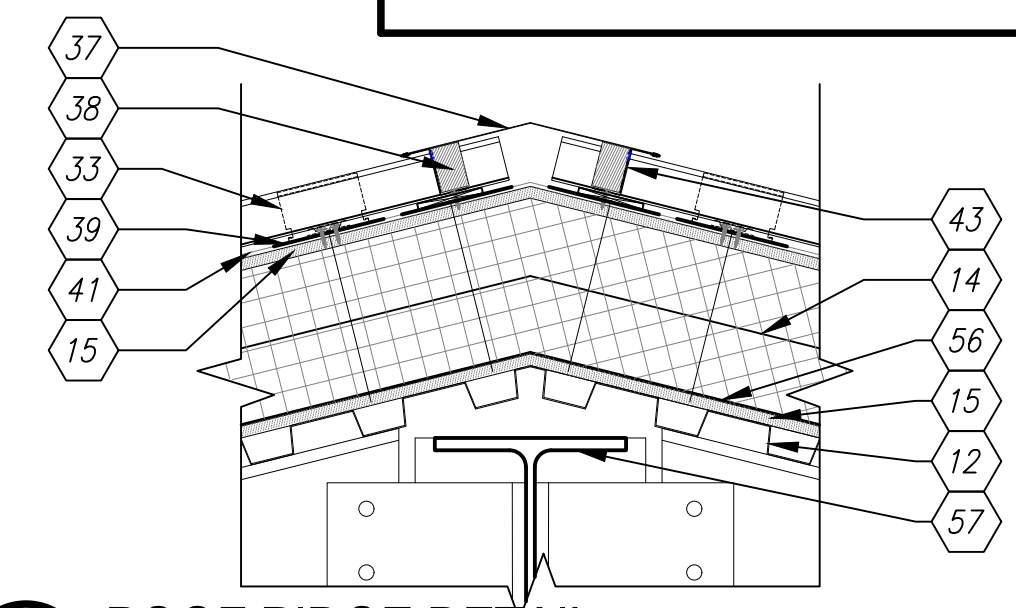

A5 ROOF RIDGE DETAIL
SCALE: 1:10
A-305

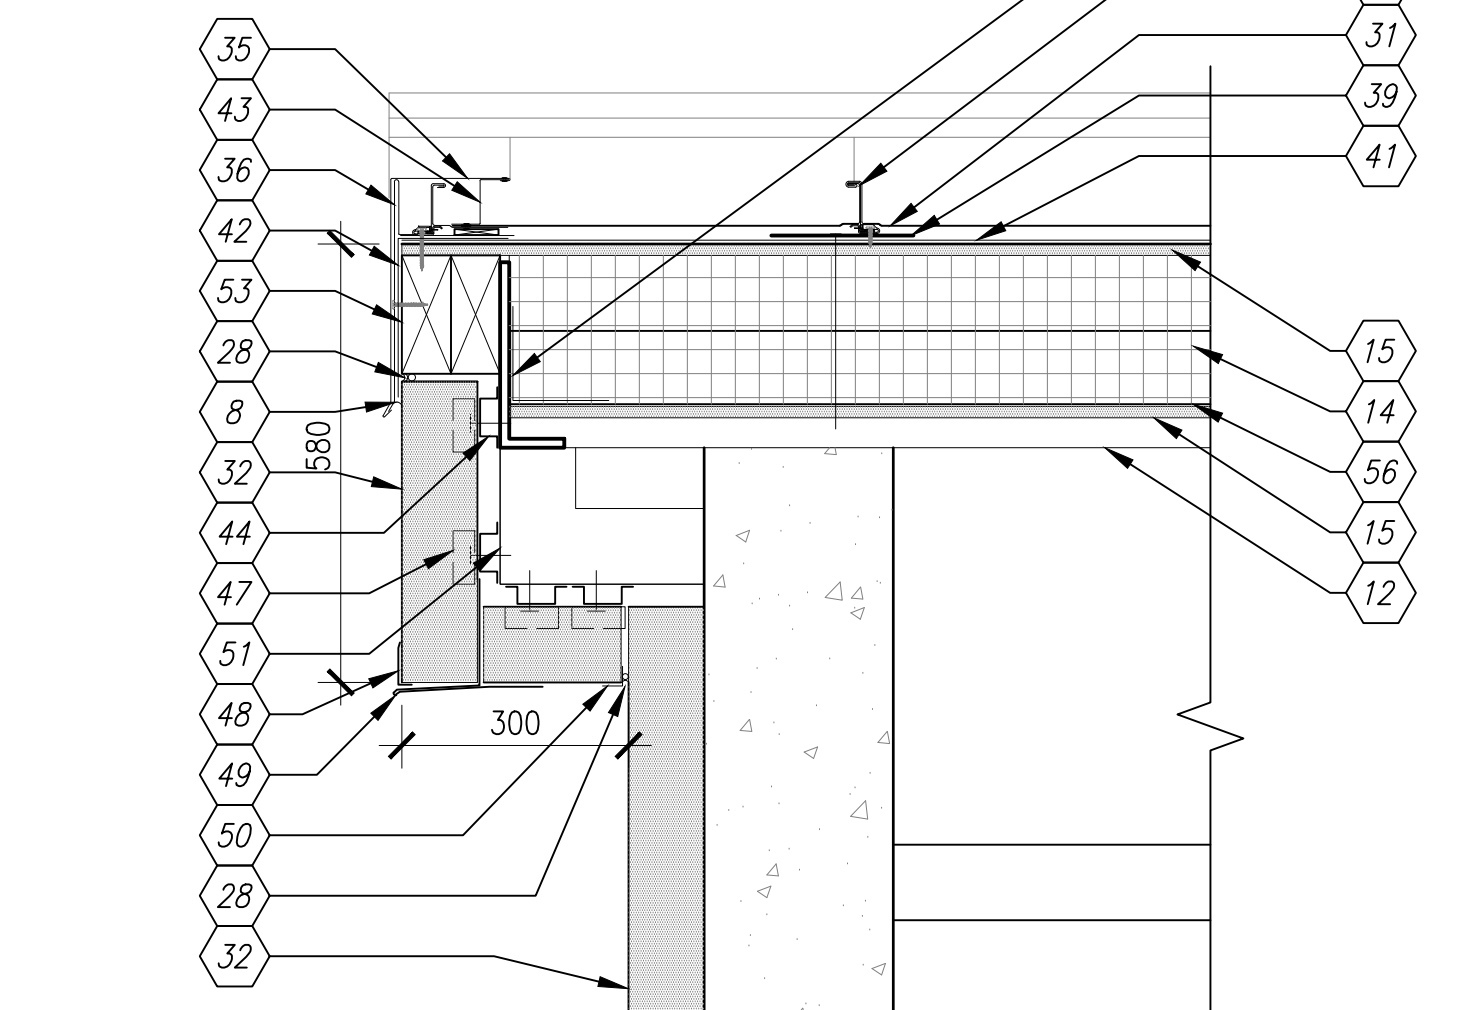


A5 HIGH ROOF RAKE DETAIL
SCALE: 1:10
A-307

GENERAL SHEET NOTES

A. FOR SBS MODIFIED BITUMEN ROOFING DETAILS NOT NOTED, REFER TO DETAIL C1/A-501 FOR KEYNOTES.

B. REFER TO SHEET A-501 FOR KEYNOTES THIS SHEET

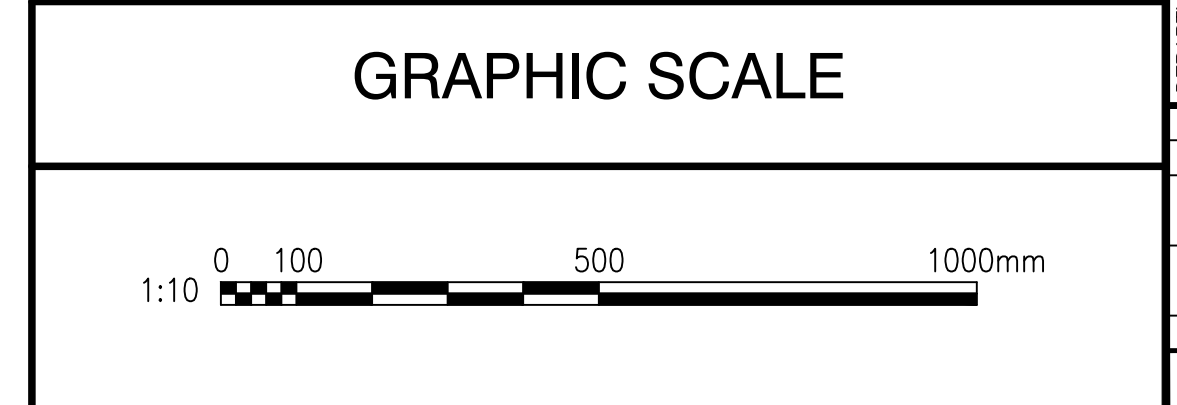

APPR	DATE	SYN	DESCRIPTION
APPROVED			
FOR COMMANDER NAVFAC			
ACTIVITY			
D. EVANS VIA EMAIL			
SATISFACTORY TO DATE 01/15/2026			
DES	PAK	DRW	PAK
PM/DM			JHR
BRANCH MANAGER MJD/ATP			
DES PROD DIR KMC			
FIRE PROTECTION ENGINEER WBF			
DSN			
NAVAL FACILITIES ENGINEERING SYSTEMS COMMAND			
NAVAL FACILITIES ENGINEERING SYSTEMS COMMAND - ATLANTIC			
PLANNING, DESIGN AND CONSTRUCTION			
VARIOUS LOCATIONS			
VARIOUS LOCATIONS			
JOINT MARITIME FACILITY			
ROOF DETAILS			
SCALE: AS NOTED			
APPROVED NO. 1838720			
CONSTR. CONTR. NO.			
NAVFAC DRAWING NO. 14157137			
SHEET 75 OF 170			
A-505			

NAVFAC METRIC DRAWING REVISION: 01 OCTOBER 2018