

9. SEALANT SHALL BE PROVIDED AT THE INTERIOR AND EXTERIOR PERIMETER OF ALL WINDOWS, DOORS AND OTHER PENETRATIONS THROUGH EXTERIOR WALLS.
10. SUFFICIENT GROUND CRACKS SHALL BE REPAIRED TO SUCH A DEGREE AS TO PREVENT FURTHER CRACKING FROM EACH MAJOR REPAIRABLE WALL, IN EACH DIRECTION, WITHIN LESS THAN 6" UNLESS OTHERWISE INDICATED.
11. WOOD USED FOR CHOKES ON TOP OR PIERCEDS ON OR ABOVE THE ROOF DECK WITHIN 8' OF ANY JOINTS OR OTHER CONNECTIONS TO THE BUILDING FRAMEWORK SHALL BE PROTECTED BY THE WEATHER SHIELD AS SPECIFIED TREATMENT LUMBER OR PVDFWOOD.
12. INSTALL ALL WORK TO BE INSURED AND VERIFY EXACT LOCATION AND ELEVATIONS FOR THE JOB.
13. DO NOT SCALE DRAWINGS. REFER TO DIMENSIONS AND SPECIFICATIONS. CONTACT THE ARCHITECT IF ADDITIONAL DIMENSIONS ARE REQUIRED.
14. CONFORM TO ALL CODE HANDBOOKS, TRADE PRICES AND TO MEET RETENT AND COMPLIANCE.
15. FIRST FLOOR LEVEL DATA ELEVATION (P) IS EQUAL TO BENCHMARK ELEVATION (P) MINUS FINISHED FLOOR ELEVATION (P) PLUS FINISHED FLOOR LEVEL DATA ELEVATION (P).
16. FLOOR LEVELS AND CEILING FINISH MATERIAL REQUIREMENTS PRIOR CLASSIFICATIONS IN ACCORDANCE WITH ASTM ARE AS FOLLOWS:
INTERNAL AND EXTERIOR PARTITION WALLS - CLASS B
FOR EXPOSED CORNERS AND OTHER SPECIAL CASES - CLASS C
ROOF AND FLOOR FINISHED SURFACES - CLASS B

	VISIBLE ITEMS
	CENTER LINE OR COLUMN GRID
	HIDDEN OR NOT IN CONTRACT
	BREAK LINE
	OVERHEAD

	BRICK FACE
	C.M.U. WALL / PARTITION - SEE PARTITION TYPES
	METAL STUD PARTITION - SEE PARTITION TYPES
	EXISTING WALL CONSTRUCTION

A		G	
AB	Area	GA	Gauge, Gage
AC	Acetate	GAU	Gauzeband
ABV	Alcohol	GC	General Contractor
KCC	Access	GCE	Glass
ACQUST:	Acoustic	GL BLK:	Gloss Black
KCP	Acrylic	GNED	Ground
ACCT	Account	GRD	Grating
ACT	Action	GRL	Gravel
ACC	Accessory	GAL	Gallon
DZ	Address Data	OIP D2	Oxygen Bottle
ADH	Adhesive		
ADJ	Adjust, Adjustable, Adjuster		
AF	After Finished Part		
AGGE:	Aggregate		
BLT	Alternate	HCCP	Handicapped [better called "Accessibility"]
ALLINE	Alliance	HCHW	Hardwood
ANGD:	Angular	CNFD	Conform
AP	Approved	HETL	Height
APPX:	Approximate	HLC	Hot/Low Melting
ATC:	Acoustical Tile Ceiling	HCRZ:	Horizontal
		HHR	Hour
		HMC	Hardwood

[illegible]

CK	Cooking	M	Moment
CL	Clack	MN	Manner
CLC	Clack	MN	Maintenance
CLD	Clack	MN	Manual
CLF	Clack	MN	Material
CLG	Clack	MN	Material
CLH	Clack	MN	Material
CLJ	Clack	MN	Material
CLK	Clack	MN	Material
CLL	Clack	MN	Material
CLM	Clack	MN	Material
CLN	Clack	MN	Material
CLP	Clack	MN	Material
CLQ	Clack	MN	Material
CLR	Clack	MN	Material
CLS	Clack	MN	Material
CLT	Clack	MN	Material
CLU	Clack	MN	Material
CLV	Clack	MN	Material
CLW	Clack	MN	Material
CLX	Clack	MN	Material
CLY	Clack	MN	Material
CLZ	Clack	MN	Material
CLAA	Clack	MN	Material
CLAB	Clack	MN	Material
CLAC	Clack	MN	Material
CLAD	Clack	MN	Material
CLAE	Clack	MN	Material
CLAF	Clack	MN	Material
CLAG	Clack	MN	Material
CLAH	Clack	MN	Material
CLAI	Clack	MN	Material
CLAJ	Clack	MN	Material
CLAK	Clack	MN	Material
CLAL	Clack	MN	Material
CLAM	Clack	MN	Material
CLAN	Clack	MN	Material
CLAO	Clack	MN	Material
CLAP	Clack	MN	Material
CLAQ	Clack	MN	Material
CLAR	Clack	MN	Material
CLAS	Clack	MN	Material
CLAT	Clack	MN	Material
CLAU	Clack	MN	Material
CLAV	Clack	MN	Material
CLAW	Clack	MN	Material
CLAX	Clack	MN	Material
CLAY	Clack	MN	Material
CLAZ	Clack	MN	Material
CLBA	Clack	MN	Material
CLBB	Clack	MN	Material
CLBC	Clack	MN	Material
CLDV	Clack	MN	Material
CLDW	Clack	MN	Material
CLDX	Clack	MN	Material
CLDY	Clack	MN	Material
CLDZ	Clack	MN	Material
CLEA	Clack	MN	

[illegible][illegible]

	ENGINEERING
	MIRA MECHANICAL & CIVIL Small 10/10/10 CHESTER PHOENIX FAX MR P

P

P. LAM	Plastic Laminate
PAR	Parallel
PERC	Perforate Board
PERIM	Perimeter
PERP	Perpendicular
PL	Plug
PLBG	Plumbing
PLYBG	PLYwood
PLUMB	Plumbing
PPR	Pipe
PREFAB	Prefabricated
PRS	Pressure
PRESS	Pressure
PRESSD	Pressurized
PSF	Pounds per square foot
PSI	Pounds per square inch
PT	Paint
PTD	Painted, Paper Towel Dispenser
PTD/R	Combination Paper Towel Dispenser/Recyclator
PTM	PATCH TO MATCH
RAISU	

Q	
QUAL	Quality
QT	Quarry Tile, Quat
QTY	Quantity
R	
RB	Rubber Base
REF	Reflecting Ceiling Pan
REFD	Reel Drum, Round, Rectoplastic Distribution Pan
REFB	Reflecting Bar
REFR	Refr., Electric, Refrigerator
REFL	Reflected,
REFP	Refrigerator, Refrigerator
REFR	Refrigerant, or Refrigerate
REQD	Required
REEL	Reel
RF	Roof
RF	Rough
RGH OPNG	Rough Opening
RGH	Rough Opening
RT	Rubber Tile
S	

SALV.	Salvage
SCHED.	Schedule
SF	Square Foot
SHR.	Showed
SH:1	Sheet
SPEC.	Specification, Specifications
SP:1	Specifications
SQ.	Square
SS	Stainless Steel
STC	Sound Transmission Class
STD.	Standard
STL	Steel
STOR.	Storage
STR:	Storage
STRUC.	Structural
STRUCT:	Structural
SURF.	Surface
SUSP.	Suspended, Suspend

T

T&R	Top and Bottom
T&G	Tongue & Groove
TS:	Towel Bar
TC	Trench Channel
TERP.	Terrazzo
THK.	Thick, Thickness
THRU:	Through
TL:	Toilet
TPD:	Toilet Paper Dispenser
TPH:	Toilet Paper Holder

TPFN:	Told Partition
TPF:	Typical
TZ:	Tenazone
U	
UNFR:	Unfinished
UNO:	Unless Noted Otherwise
UNR:	Unless Otherwise Noted
UP:	Unpainted
UR:	Unreal
V	
VAT:	Vinyl Asbestos Tile
VBC:	Vinyl Base (Concrete)
VCT:	Vinyl Composition Tile
VFR:	Vertical
VECT:	Vesiculate
VF:	Very In This Field
VF:	Vinyl Tile
VTR:	Vent Through Roof
VWC:	Vinyl Wall Covering
W	
W:	Width

WC:	Without
WC&E:	Watercast
WC:	Watercoul
WC:	Wood

	CONCRETE MASONRY UNITS (CMU)		WOOD (FINISHED)
	CONCRETE		WOOD (ROUGH)
	BRICK		WOOD (BLOCKING)
	CEMENT, SAND, GROUT, PLASTER, OR GYPSUM WALL BOARD		PARTICLE BOARD
	STEEL		PLYWOOD

	WALL TYPE	
	DEMO KEYNOTE	
	PLANE/ELEVATION KEYNOTE	
	FINISH KEYNOTE	

The diagram illustrates the horizontal alignment of three vertical elements relative to a common horizontal line. From left to right, the elements are: a square column, a hatched wall/partition, and a vertical line representing a gypsum board/stud partition. Vertical dashed lines connect each element to its corresponding label below. The labels are: 'CENTER LINE OF COLUMN (U.O.N.)', 'NOMINAL FACE OF MASONRY AND CONCRETE WALL / PARTITIONS', and 'NOMINAL FACE OF GYP AT GYP BO/STUD PARTITION'.

1. DASHED LINES INDICATE ITEMS TO BE REMOVED.
2. ELEMENTS TO REMAIN IN PLACE SHALL BE PROTECTED FROM DAMAGE, DUST AND DEBRIS.
3. DUST CONTROL SHALL BE THE FULL RESPONSIBILITY OF THE CONTRACTOR. CONTRACTOR SHALL PERFORM CLEAN UP OF ALL REFUSE, RUBBISH, SCRAP MATERIALS AND DEBRIS CAUSED BY THE WORK & DUST, CLEANING OF AREA SURROUNDING THE WORK AREA WHERE CONSTRUCTION DEBRIS OR DUST ACCUMULATES WILL BE THE RESPONSIBILITY OF THE CONTRACTOR.
4. REFER TO STRUCTURAL, MECHANICAL, ELECTRICAL AND PLUMBING DRAWINGS FOR DEMOLITION OF ADDITIONAL ITEMS.

1. CONSTRUCTION SHALL CONFORM TO THE CODES GOVERNED BY THE JURISDICTION IN WHICH THE PROJECT IS BEING CONSTRUCTED.
2. CONSTRUCTION SHALL COMPLY WITH ALL LOCAL, STATE AND FEDERAL CODES AND REGULATIONS.
3. ALL DRAWINGS ARE GRAPHIC REPRESENTATIONS OF APPROXIMATE LOCATIONS OF NEW MATERIALS. IT IS THE CONTRACTOR'S RESPONSIBILITY TO FIELD VERIFY ALL CONDITIONS PRIOR TO COMMENCEMENT OF WORK.
4. CONTRACTORS ARE RESPONSIBLE FOR ALL MATERIALS, CONSTRUCTION METHODS AND CRAFTSMANSHIP.
5. CONTRACTORS ARE TO VERIFY ALL EXISTING CONDITIONS, REQUIREMENTS, NOTES, CODES AND DIMENSIONS, PRIOR TO THE

[illegible]

 LaBella
Powered by partnership.

300 State Street | Engineering
Suite 201 | Architecture
Rochester, NY 14614 | Environmental
P: (585) 454-6110 | Planning
www.labellapc.com

Miller-Remick LLC
M.E.P. & Structural Engineering
A Service Disabled Veteran Owned
Small Business

1010 KINGS HIGHWAY SOUTH
CHERRY HILL, NEW JERSEY 08034
PHONE: (856)429-4000
FAX: (856)429-5002
MR PROJECT NO: 0507-0014

Office of
Construction
and Facilities
Management


 U.S. Department
of Veterans Affairs

Drawing Title
ARCHITECTURAL NOTES, SYMBOLS & ABBREVIATIONS
Approved: Project Director

Phase	CONSTRUCTION BID DOCUMENTS
	NON-SPRINKLERED

Project Title		
UD CHILLER CAPACITY UPGRADE		
Location UNIVERSITY DRIVE CAMPUS PITTSBURGH, PENNSYLVANIA		
Issue Date	Checked	Dra
2022-05-11	TM	

Project Number	646-20-109
Building Number	8
Drawing Number	AE001

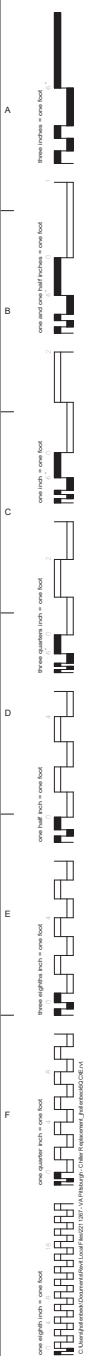

F

one quarter inch = one foot

0 4 8 16

one eighth inch = one foot

0 4 8 16

C. Used for book Documental Nova Local # A2271-1987 - VA Pittsburgh-Center Replacement, July 1988.

A FORM 08-6231

 **LaBella**
Powered by partnership.

300 State Street
Suite 201
Rochester, NY 14614
P: (585) 454-6110

Engineering
Architecture
Environmental
Planning

www.labellapc.com




Miller-Remick LLC
M.E.P. & Structural Engineering
A Service Disabled Veteran Owned
Small Business


1010 KINGS HIGHWAY SOUTH
CHERRY HILL, NEW JERSEY 08034
PHONE: (856)429-4000
FAX: (856)429-5002
MR PROJECT NO: 0507-0014

VA U.S. Department
of Veterans Affairs

Drawing Number	AD101
----------------	-------

	EXISTING WALL TO BE REMOVED
	EXISTING DOOR AND FRAME TO BE REMOVED
	EXISTING WALL TO REMAIN
	EXISTING DOOR TO REMAIN
	PORTIONS OF SLAB TO BE REMOVED; SEE STRUCTURAL DRAWINGS

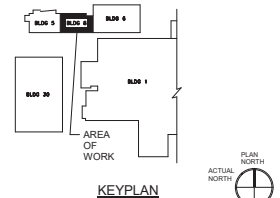[illegible]


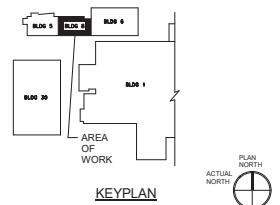
[illegible]

WITNESS THIS DRAWING SHALL NOT BE USED FOR ANY PURPOSE WHATSOEVER WITHOUT THE SEAL AND SIGNATURE OF THE PROFESSIONAL ENGINEER.		CONSULTANT  LaBella Powered by partnership. 301 State Street Exeter, NH 03824 Phone: (603) 441-1111 Fax: (603) 441-1112 Email: info@labella.com Website: www.labella.com		ENGINEER OF RECORD  Miller-Remick LLC M.E.P. & Structural Engineering A Service Disabled Veteran Owned Small Business 1010 KINGS HIGHWAY SOUTH CHERRY HILL, NEW JERSEY 08034 PHONE: (609) 766-7000 FAX: (609) 766-7001 MR PROJECT NO. 0507-0014		ARCHITECT'S STAMP 		Office of Construction and Facilities Management  U.S. Department of Veterans Affairs		Drawing Title ARCHITECTURAL DEMOLITION PLAN - SECOND LEVEL		Phase CONSTRUCTION BID DOCUMENTS		Project Title UD CHILLER CAPACITY UPGRADE		Project Number 645-20-109	
								Approved: Project Director		NON-SPRINKLERED		Location UNIVERSITY DRIVE CAMPUS PITTSBURGH, PENNSYLVANIA		Building Number 8			
NO. DESCRIPTION DATE										Issue Date 2022-05-11		Checked TM		Drawn JH, WM			
IN FORM 08-0231												Drawing Number AD102					

DEMO NOTED	
01	REMOVE EXISTING FLOOR & PORTIONS OF FOUNDATION. REFER TO STRUCTURAL DWGS FOR FULL EXTENT OF REMOVAL.
02	REMOVE EXISTING STRUCTURAL STEEL FRAME. REFER TO STRUCTURAL DWGS FOR MORE INFORMATION.
03	REMOVE EXISTING CORN. BEARING WALL. WALL TO BE DEMOLISHED AFTER ROOF CONSTRUCTION HAS BEEN REMOVED. REFER TO STRUCTURAL DWGS.
04	REMOVE EXISTING PARTITION. PATCH TO MATCH ANY WALLS AFFECTED BY DEMO WORK.
05	REMOVE EXISTING DOOR, HARDWARE & FRAME. PATCH TO MATCH ANY WALLS AFFECTED BY DEMO WORK.
06	REMOVE EXISTING DUCTWORK. REFER TO MEP DRAWINGS FOR FURTHER INFORMATION.
07	REMOVE EXISTING MECHANICAL EQUIPMENT. REFER TO MEP DRAWINGS FOR FURTHER INFORMATION.
08	REMOVE EXISTING LADDER CASE. REFER TO STRUCTURAL DRAWINGS FOR FURTHER INFORMATION.
09	REMOVE EXISTING MASSORY WALL. BE REMOVED AFTER DEMOLITION OF EXISTING WALLS. REFER TO STRUCTURAL DRAWINGS.
10	REMOVE EXISTING EQUIP. PADS. REFER TO STRUCTURAL DWGS FOR FURTHER INFORMATION.
11	REMOVE EXISTING FINISH CEILING. REFER TO MEP DRAWINGS FOR FURTHER INFORMATION.
12	REMOVE EXISTING ROOFING SYSTEM & STRUCTURAL MEMBERS. REFER TO STRUCT DWGS FOR FURTHER INFORMATION.
13	REMOVE EXISTING WALLS AS NOTED. PATCH EXISTING WALLS & ROOF AS REQUIRED.
14	REMOVE PORTION OF BLG AS NOTED FOR RELOCATED FLOOR DRILL. SEE STRUCTURAL & PLUMBING DWGS.
15	REMOVE EXISTING WALL. PATCH REFER TO MEP DRAWINGS FOR ADDITIONAL INFORMATION. PREP WALL TO BE FIN.
16	REMOVE EXISTING CORNER & BRICK PARAPET DOWN TO EXISTING WALL.
17	REMOVE EXISTING ROOFING & BRICK PARAPET WALL WHERE WALL BELOW IS DEMO. COORDINATE WITH STRUCTURAL DRAWINGS.
18	REMOVE EXISTING ROOF FOR NEW THROUGH ROOF PENETRATIONS. SEE SPACE STRUCTURAL DRAWINGS FOR ADDITIONAL INFORMATION.
19	REMOVE COPING AND BLOCKING DOWN TO EXISTING CMU BLOCK WALL. DO NOT DISTURB EXISTING ROOFING.

- ### GENERAL REMOVAL NOTES:
- DASHED LINES INDICATE ITEMS TO BE REMOVED.
 - ELEMENTS TO REMAIN IN PLACE SHALL BE PROTECTED FROM DAMAGE, DUST AND DEBRIS.
 - DUST CONTROL SHALL BE THE FULL RESPONSIBILITY OF THE CONTRACTOR. CONTRACTOR SHALL FORM A CLEAN UP OF ALL DUST. REMOVE DEBRIS MATERIALS AND DEBRIS CAUSED BY THE WORK ON A DAILY BASIS. CLEANING OF AREA SURROUNDING THE WORK AREA WHERE CONSTRUCTION DEBRIS OR DUST ACCUMULATES SHALL BE THE RESPONSIBILITY OF THE CONTRACTOR.
 - REFER TO STRUCTURAL, MECHANICAL, ELECTRICAL & PLUMBING DRAWINGS FOR DEMOLITION OF ADDITIONAL ITEMS.
 - CONTRACTOR TO MAINTAIN WATER TIGHT INTEGRITY OF BUILDING AT ALL TIMES.
 - EXISTING CONDITIONS ARE TAKEN FROM FIELD OBSERVATIONS AND PRIOR CONSTRUCTION DOCUMENTS. WHERE AVAILABLE AND ARE NOT QUANTIFIED, CONTRACTORS ARE RESPONSIBLE FOR EXAMINING THE BUILDING AND NOTING EXISTING CONDITIONS AND ARE TO CONTACT THE OWNER REPRESENTATIVE REGARDING ANY DISCREPANCIES.
 - DEMOLITION WORK SHALL INCLUDE REMOVAL OF ALL ITEMS INDICATED TO BE REMOVED AND/OR SALVAGED, AND LEGAL DISPOSAL OF ITEMS NOT INTENDED FOR SALVAGE. WORK SHALL ALSO INCLUDE REMOVAL OF ALL BRICKS, SUPPORTS, BRACKETS, FASTENERS, CONCRETE, FINISH, AND SIMILAR ITEMS WHICH ARE NOT INDICATED TO REMAIN.
 - ALL FLOOR AND WALL CONDITIONS WHICH ARE TO RECEIVE NEW CONSTRUCTION ARE TO BE DEMOLISHED AS BACKDROPPED AND PROPERLY PREPARED TO RECEIVE NEW FINISHES, I & D.
 - ALL FLOOR, WALL, AND CEILING CONDITIONS THAT ARE DISTURBED BY DEMOLITION ARE TO BE PATCHED, REFINISHED AND/OR PAINTED WITH SIMILAR MATERIALS AND COLORS. REFER TO NEW WORK FLOOR PLANS, REFLECTED CEILING PLANS, AND FINISH SCHEDULE.
 - AT WALL REMOVAL FOR MECHANICAL PENETRATIONS, OPENING TO BE APPROXIMATELY 8" LARGER THAN DUCT SIZE OR ALL SIZES, CORRESPONDING WITH MECHANICAL DRAWINGS.
 - FOR ADDITIONAL REMOVAL INFORMATION REFER TO SECTIONS AND DETAILS.
 - WORK AREAS WERE SURVEYED TO IDENTIFY HAZARDOUS MATERIALS. REFER TO MARBETT & ASSOCIATES REGULATED BUILDING MATERIALS SURVEY REPORT FOR VA PROJECT NO. 646-20-108, PITTSBURGH NAME: MARBETT & ASSOCIATES, LLC. DESIGN SERVICES FOR PITTSBURGH NAME: US CHILLER CAPACITY AND CONTROLS UPGRADE DATED APRIL 2, 2021 FOR ADDITIONAL INFORMATION. NOT ALL AREAS MAY HAVE BEEN ACCESSIBLE AND HAZARDOUS MATERIALS MAY EXIST IN AREAS NOT BEEN IDENTIFIED. IF SUSPECT MATERIALS ARE DISCOVERED WHICH HAVE NOT BEEN PROBABLY IDENTIFIED, THE CONTRACTOR SHALL NOT DISTURB THOSE MATERIALS AND SHALL IMMEDIATELY NOTIFY THE CDR.
 - OSHA LEAD REGULATIONS WILL APPLY TO ANY DEMOLITION OPERATION (I.E. SANDING, SCRAPING, CUTTING, AND MILLING) THAT WOULD DISTURB PAINTED SURFACES WHICH CONTAIN LEAD. OCCUPATIONAL EXPOSURE TO LEAD IS REGULATED BY OSHA (29 CFR 1910.1025) AS WELL AS APPLICABLE STATE REGULATIONS. DISPOSAL OF MATERIALS COATED WITH PAINT CONTAINING LEAD IS SUBJECT TO THE USEPA RESOURCE CONSERVATION AND RECOVERY ACT (RCRA) REGULATIONS. REFER TO SPECIFICATIONS FOR FURTHER INFORMATION.


- ### REMOVAL LEGEND:
- EXISTING WALL TO BE REMOVED
 - - - - - EXISTING DOOR & FRAME TO BE REMOVED
 - EXISTING WALL TO REMAIN
 - - - - - EXISTING DOOR TO REMAIN
 - PORTIONS OF BLG TO BE REMOVED: SEE STRUCTURAL DRAWINGS

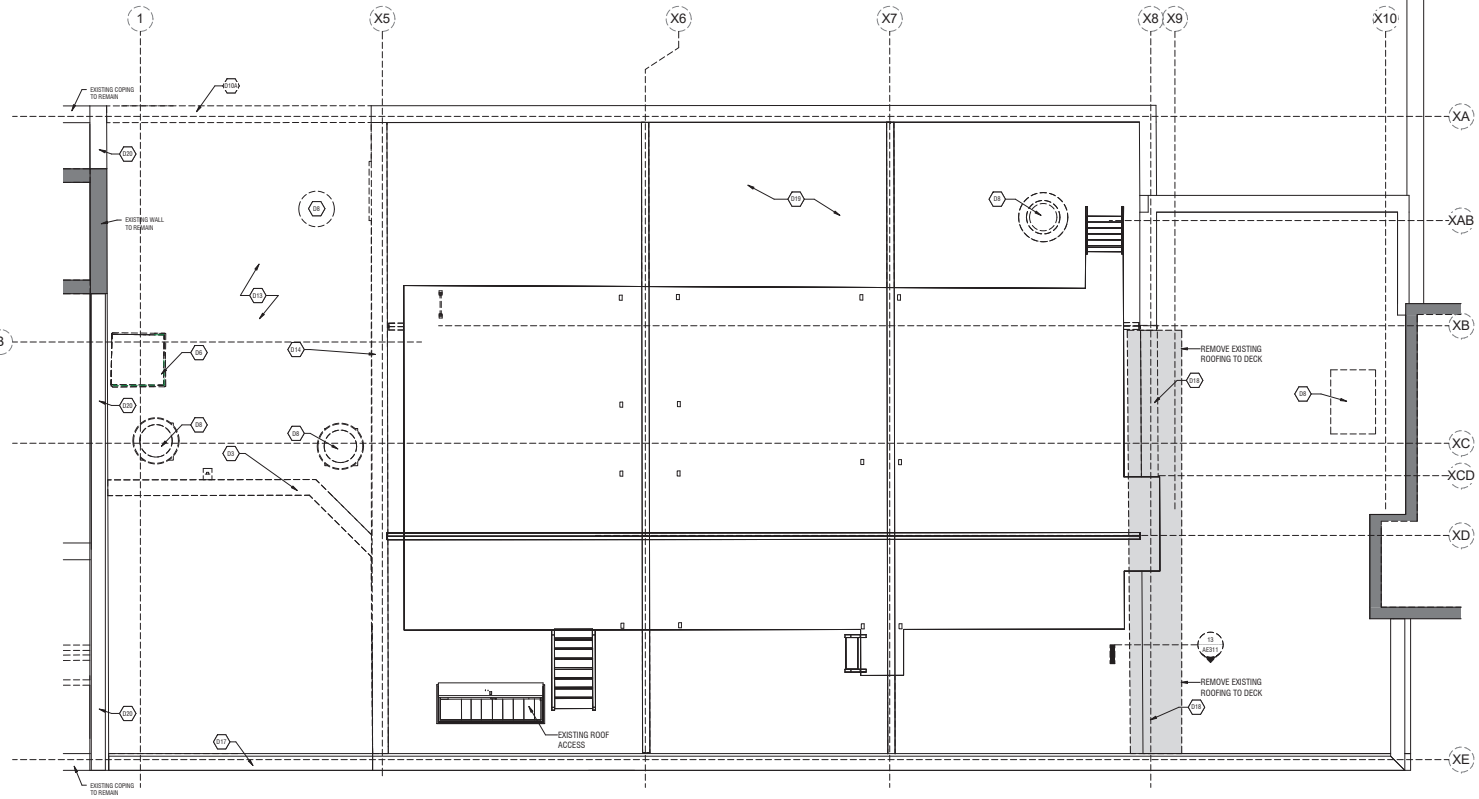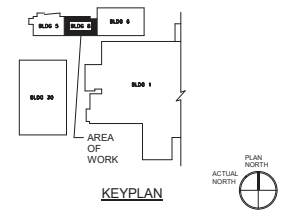

1 ROOF LEVEL DEMOLITION PLAN
SCALE: 1/4" = 1'-0"

PRINTS OF THIS DRAWING SHALL NOT BE USED FOR ANY PURPOSE WHATSOEVER WITHOUT THE SEAL AND SIGNATURE OF THE PROFESSIONAL ENGINEER.		CONSULTANT LaBella Powered by partnerships. 300 State Street Engineering Suite 201 Architecture Rochester, NY 14614 Environmental P (585) 451-6110 Planning www.labellagroup.com		ENGINEER OF RECORD Miller-Remick LLC M.E.P. & Structural Engineering A Service Disabled Veteran Owned Small Business 1010 KINGS HIGHWAY SOUTH CHERY HILL, NEW JERSEY 08034 PHONE: (856) 429-4000 FAX: (856) 429-5002 NY PROJECT NO. 0489-0014		ARCHITECT'S STAMP 		Office of Construction and Facilities Management VA U.S. Department of Veterans Affairs		Drawing Title ARCHITECTURAL DEMOLITION PLAN ROOF LEVEL Approved: Project Director		Phase CONSTRUCTION BID DOCUMENTS NON-SPRINKLERED		Project Title UD CHILLER CAPACITY UPGRADE Location UNIVERSITY DRIVE CAMPUS PITTSBURGH, PENNSYLVANIA Issue Date 2022-05-11		Project Number 646-20-109 Building Number 8 Drawing Number AD103	
--	--	---	--	---	--	------------------------------	--	--	--	--	--	--	--	--	--	--	--


FINISH SYMBOLS LEGEND & ABBREVIATIONS

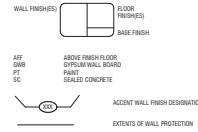

MATERIAL LEGEND


MATERIAL	NAME	MANUFACTURER	DATE	COLOR	LOCATION
PAINT	PL-1	SHERWIN WILLIAMS	09 01 23	TBD	WALL PAINT
PAINT	PL-2	SHERWIN WILLIAMS	09 01 23	SW684 SAFETY YELLOW	EQUIPMENT PAD
SCALES	SC	RETRUPLATE	03 36 00	-	CONCRETE FLOORS

GENERAL PLAN SYMBOLS:

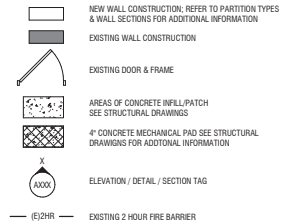


GENERAL PLAN NOTES:


- ALL DIMENSIONS TO BE TAKEN FROM FACE OF WALL UNLESS INDICATED OTHERWISE.
- JOINTS ABUTTING EXISTING WALLS ARE TO BE TAPPED AND FINISHED.
- COORDINATE NEW DATA & POWER LOCATIONS WITH OWNER AND ELECTRICAL DRAWINGS.
- CONTRACTOR SHALL PROVIDE BLOCKING AS REQUIRED FOR ALL MILLWORK AND EQUIPMENT INSTALLATION.
- FURNITURE AND EQUIPMENT TO BE PROVIDED BY OWNER. VERIFY FINAL LOCATION AND REQUIREMENTS OF ALL EQUIPMENT WITH CORP.
- PATCH ALL EXISTING WALLS AS REQUIRED; PREPARE ALL WALLS FOR PAINT.
- SEE ELECTRICAL DRAWINGS FOR NEW FIXTURES & DEVICES.

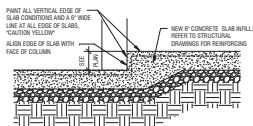


2 SLAB EDGE DETAIL
SCALE: 3/4\"/>

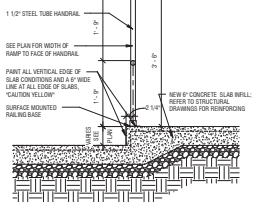

3 HANDRAIL DETAIL
SCALE: 3/4\"/>

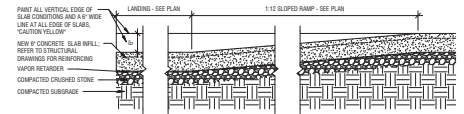

4 RAMP DETAIL
SCALE: 3/4\"/>

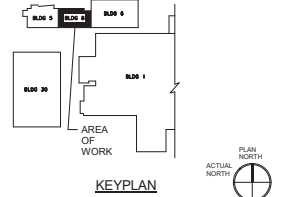

1 FIRST LEVEL FLOOR PLAN
SCALE: 1/4\"/>

PRINTS OF THIS DRAWING SHALL NOT BE USED FOR ANY PURPOSE WHATSOEVER WITHOUT THE SEAL AND SIGNATURE OF THE PROFESSIONAL ENGINEER.

CONSULTANT



ENGINEER OF RECORD



ARCHITECT'S STAMP



Office of Construction and Facilities Management



Drawing Title
ARCHITECTURAL FLOOR & FINISH PLAN - FIRST LEVEL

Approved: Project Director

Phase
CONSTRUCTION BID DOCUMENTS

NON-SPRINKLERED

Project Title
UD CHILLER CAPACITY UPGRADE

Location
UNIVERSITY DRIVE CAMPUS PITTSBURGH, PENNSYLVANIA


Issue Date
2022-05-11

Project Number
646-20-109

Building Number
8

Drawing Number
AE101


VA FORM 08-6231

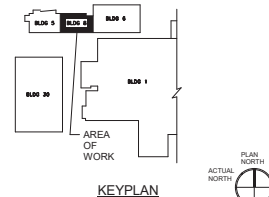


Drawing Number	AE103
----------------	-------

GENERAL NOTES:


1. ALL DIMENSIONS TO BE TAKEN FROM FACE OF WALL UNLESS INDICATED OTHERWISE.
2. SEE STRUCTURAL DRAWINGS FOR ADDITIONAL INFORMATION.

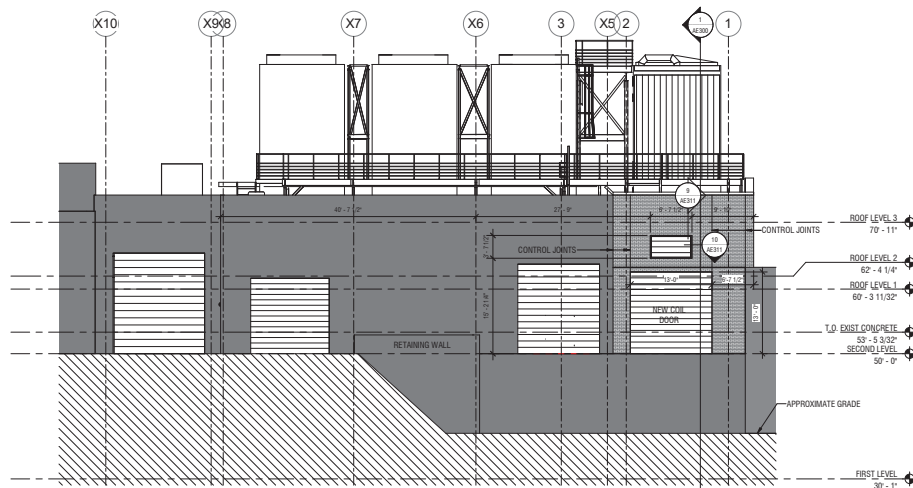

1 NORTH ELEVATION
SCALE: 1/8" = 1'-0"

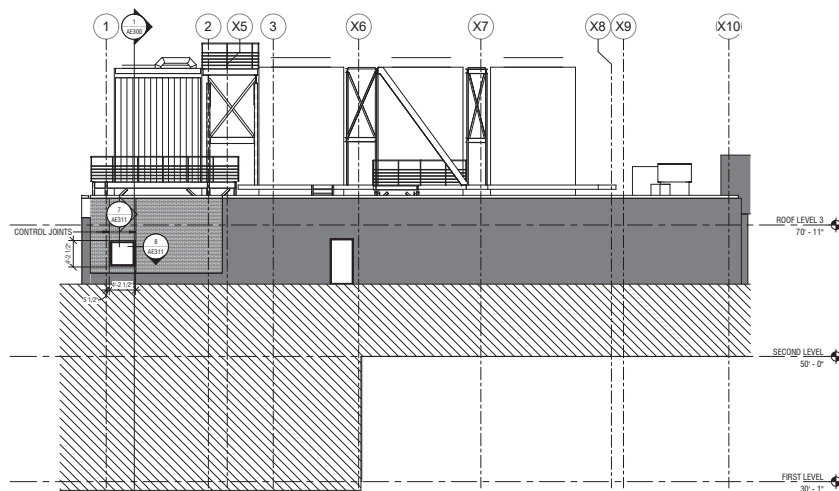

2 SOUTH ELEVATION
SCALE: 1/8" = 1'-0"

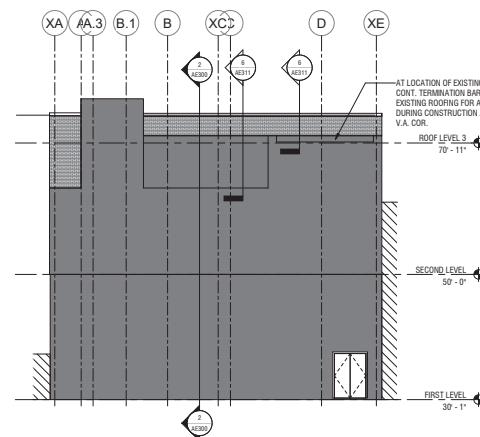

3 WEST ELEVATION
SCALE: 1/8" = 1'-0"

PRINTS OF THIS DRAWING SHALL NOT BE USED FOR ANY PURPOSE WHATSOEVER WITHOUT THE SEAL AND SIGNATURE OF THE PROFESSIONAL ENGINEER.

CONSULTANT

LaBella
POWERED BY PARTNERSHIPS.
300 State Street | Engineering
Suite 201 | Architecture
Rochester, NY 14614 | Environmental
P (585) 451-6110 | Planning
www.labella.com

ENGINEER OF RECORD

Miller-Remick LLC
M.E.P. & Structural Engineering
A Service Disabled Veteran Owned
Small Business
1010 KINGS HIGHWAY SOUTH
CHERRY HILL, NEW JERSEY 08034
PHONE: (856) 429-4000
FAX: (856) 429-5802
NJ PROJECT NO. 0507-0014

ARCHITECT'S STAMP



Office of
Construction and
Facilities
Management

VA U.S. Department
of Veterans Affairs

Drawing Title
**ARCHITECTURAL EXTERIOR
ELEVATIONS**

Approved: Project Director

Phase
**CONSTRUCTION BID
DOCUMENTS**

NON-SPRINKLERED

Project Title
**UD CHILLER CAPACITY
UPGRADE**

Location **UNIVERSITY DRIVE CAMPUS
PITTSBURGH, PENNSYLVANIA**

Issue Date **2022-05-11** Checked **TM** Drawn **JH, WM**

Project Number
646-20-109

Building Number
8

Drawing Number
AE200

1. ALL DIMENSIONS TO BE TAKEN FROM FACE OF WALL UNLESS INDICATED OTHERWISE.
2. SEE STRUCTURAL DRAWINGS FOR ADDITIONAL INFORMATION.

[illegible]

 **LaBella**
Powered by partnership.

300 State Street
Suite 201
Rochester, NY 14614
P: (585) 454-6110

Engineering
Architecture
Environmental
Planning

www.labellapc.com

 **Miller-Remick LLC**
M.E.P. & Structural Engineering
A Service Disabled Veteran Owned
Small Business

1010 KINGS HIGHWAY SOUTH
CHERRY HILL, NEW JERSEY 08034
PHONE: (856) 429-4000
FAX: (856) 429-5002
MR PROJECT NO: 0499-0014






VA U.S. Department
of Veterans Affairs

Approved: Project Director


NON-SPRINKLERED

Location	UNIVERSITY DRIVE CAMPUS PITTSBURGH, PENNSYLVANIA	
Issue Date	Checked	Drawn
2022-05-11	TM	JL


Drawing Number	AE300
----------------	-------

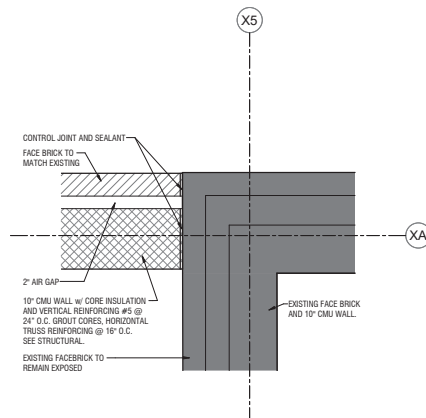


1 PLAN DETAIL
AE310 SCALE: 1 1/2" = 1'-0"

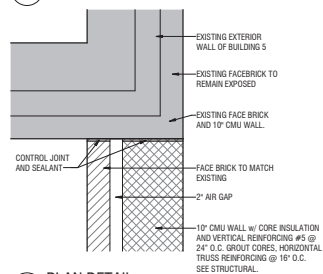

3 PLAN DETAIL
AE310 SCALE: 1 1/2" = 1'-0"

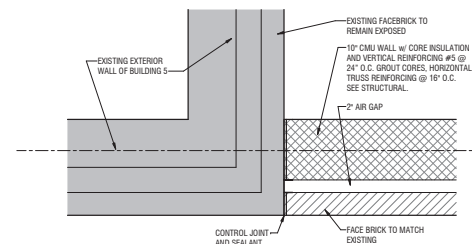

4 PLAN DETAIL
AE310 SCALE: 1 1/2" = 1'-0"

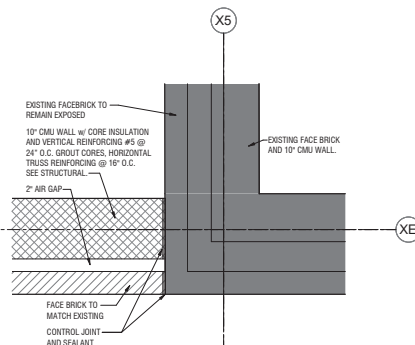

5 PLAN DETAIL
AE310 SCALE: 1 1/2" = 1'-0"

PRINTS OF THIS DRAWING SHALL NOT BE USED FOR ANY PURPOSE
WHATSOEVER WITHOUT THE SEAL AND SIGNATURE OF THE
PROFESSIONAL ENGINEER.

No.	Description	Date

CONSULTANT



300 State Street
Suite 201
Rochester, NY 14614
P: (585) 454-6110
www.jabellapp.com

ENGINEER OF RECORD



ARCHITECT'S STAMP



Office of
Construction
and Facilities
Management

U.S. Department
of Veterans Affairs

Drawing Title
ARCHITECTURAL PLAN DETAILS

Approved: Project Director

Phase	CONSTRUCTION B DOCUMENTS
-------	-----------------------------

NON-SPRINKLERED

Project Title	UD CHILLER CAPACITY UPGRADE
---------------	-----------------------------

Location	UNIVERSITY DRIVE CAMPUS CENTRAL BUILDING
----------	---

Issue Date
2022-05-11

Checked	TM
---------	----

A
Drawn

Project Number	646-20-109
----------------	------------

Building Number	8
-----------------	---

	Drawing Number
--	----------------

AE310

VA FORM 08-6231

