

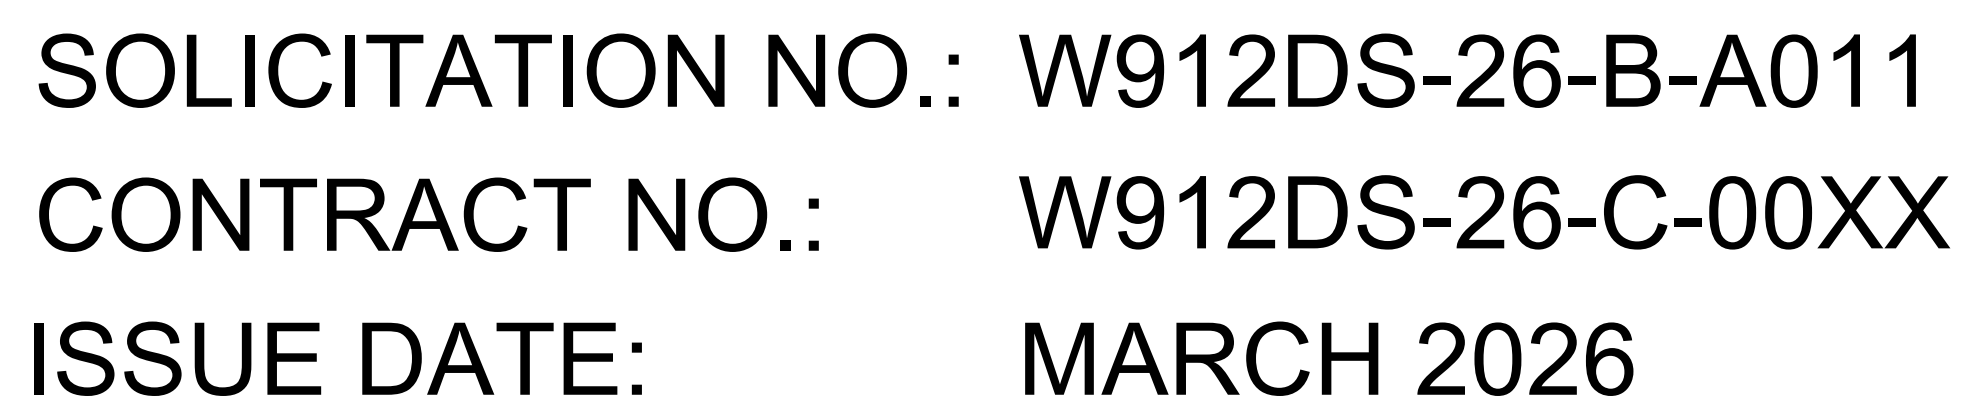


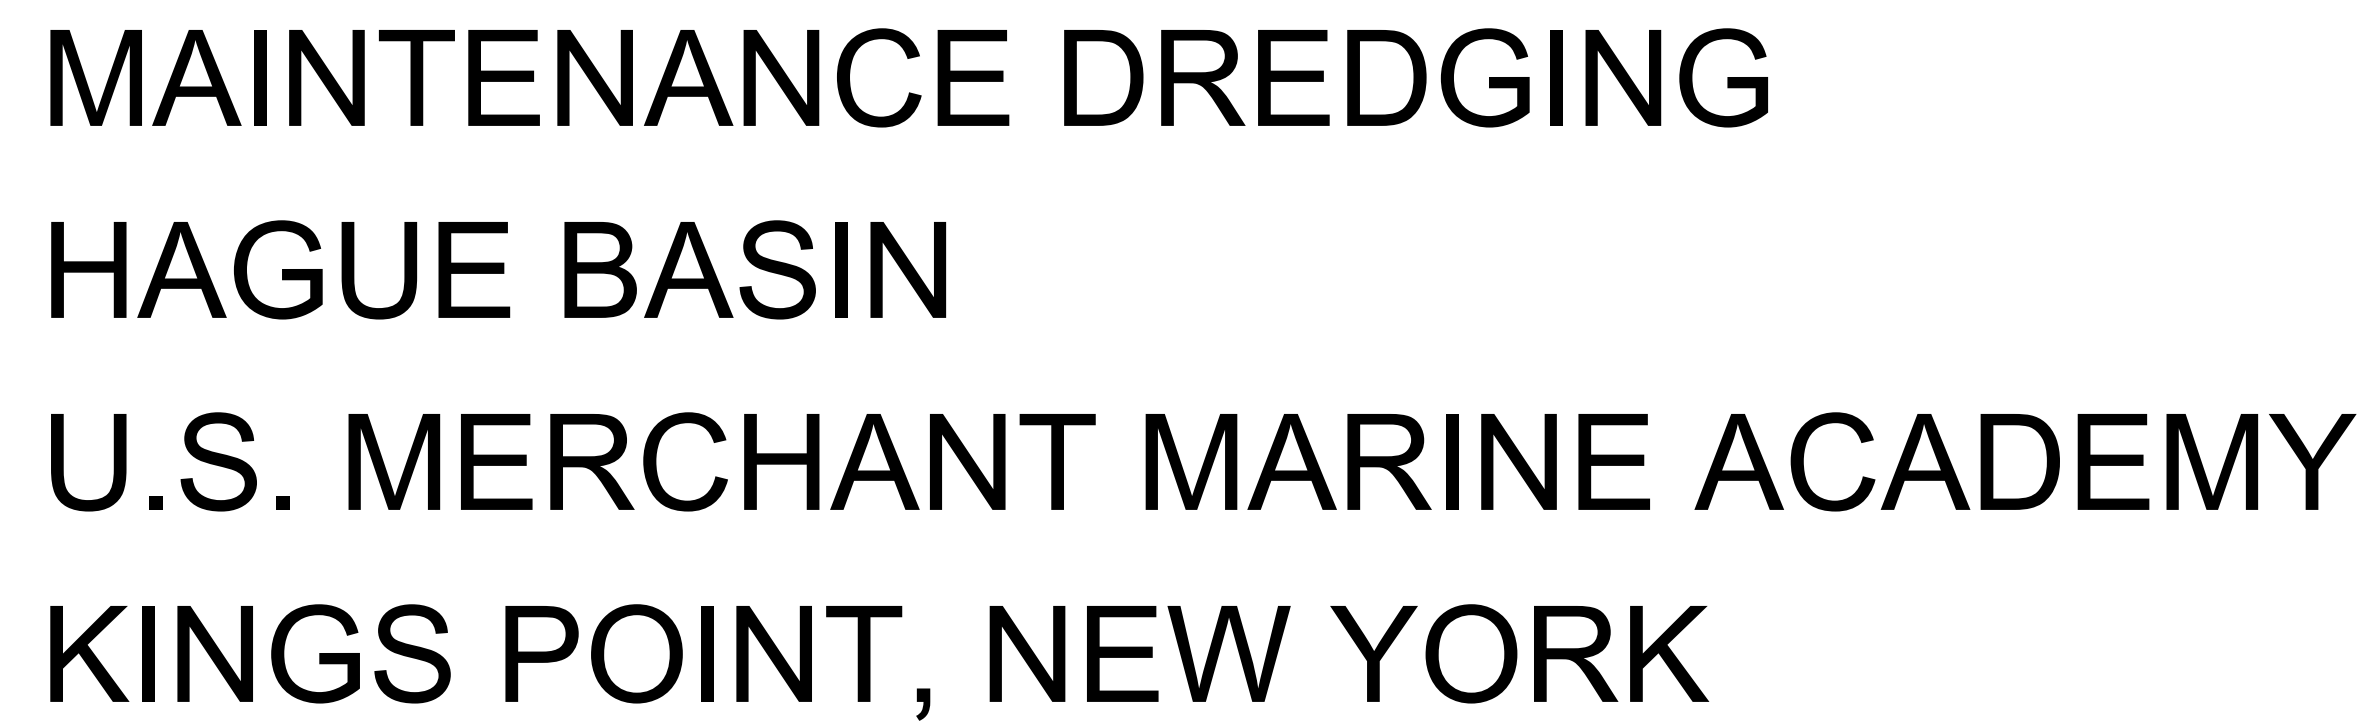

INDEX OF DRAWINGS

SHEET NUMBER	TITLE
G-001	COVER SHEET & INDEX
GI-101	PROJECT SITE PLAN & NOTES
C-101	DREDGING AREA & SOUNDING MAP

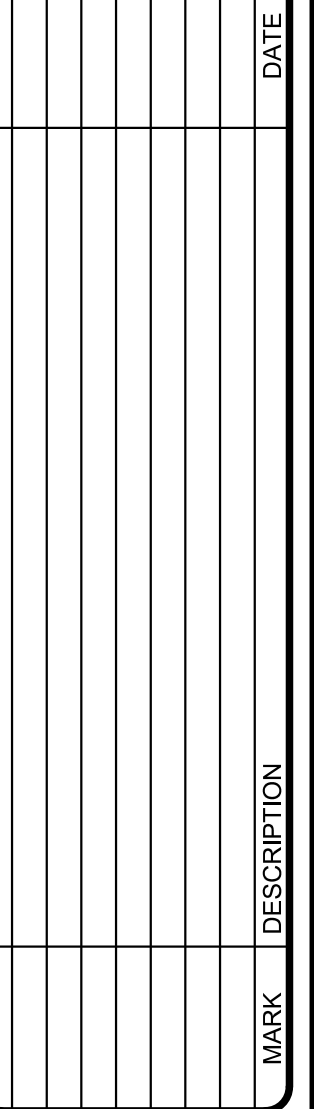


U.S. ARMY CORPS OF ENGINEERS DEPARTMENT OF THE ARMY NEW YORK, NEW YORK 10278	OPERATIONS DIVISION OPERATIONS SUPPORT BRANCH TECHNICAL SECTION CEAN-OP-ST	DAVID M. GRIFFIN DAVID M. GRIFFIN DAVID M. GRIFFIN JESSICA KONG SUBMITTED BY MICHAEL L. OSEBACK N/A	MARCH 2026 SOLICITATION NO.: W912DS-26-A011 NO. OF PAGES: 26 CDDXX SCALE N/A
--	---	---	---

MAINTENANCE DREDGING
HAGUE BASIN
U.S. MERCHANT MARINE ACADEMY
KINGS POINT, NEW YORK



COVER SHEET & INDEX

SHEET ID
G-001
1 OF 3

CHANNEL COORDINATES			
HAGUE BASIN, NY (Full Reach Coordinates)			
	EASTING	NORTHING	
1	1049129.408	234938.342	
2	1049182.150	235710.513	
3	1049207.858	235723.698	
4	1049337.015	235662.836	
5	1049331.786	235651.528	
6	1049392.767	235620.723	
7	1049333.064	235485.029	
8	1049290.734	235063.742	
9	1049421.991	235046.971	
10	1049403.170	234839.977	
11	1049356.961	234832.201	
12	1049274.043	234887.722	
13	1049252.535	234856.696	
14	1049233.955	234869.034	
15	1049261.267	235523.092	
16	1049169.624	235529.769	
17	1049435.167	235602.984	
18	1049421.679	235574.894	
19	1049386.716	235091.325	
20	1049484.185	235080.292	
21	1049471.028	234929.057	
22	1049511.736	234922.973	
23	1049508.306	234860.298	

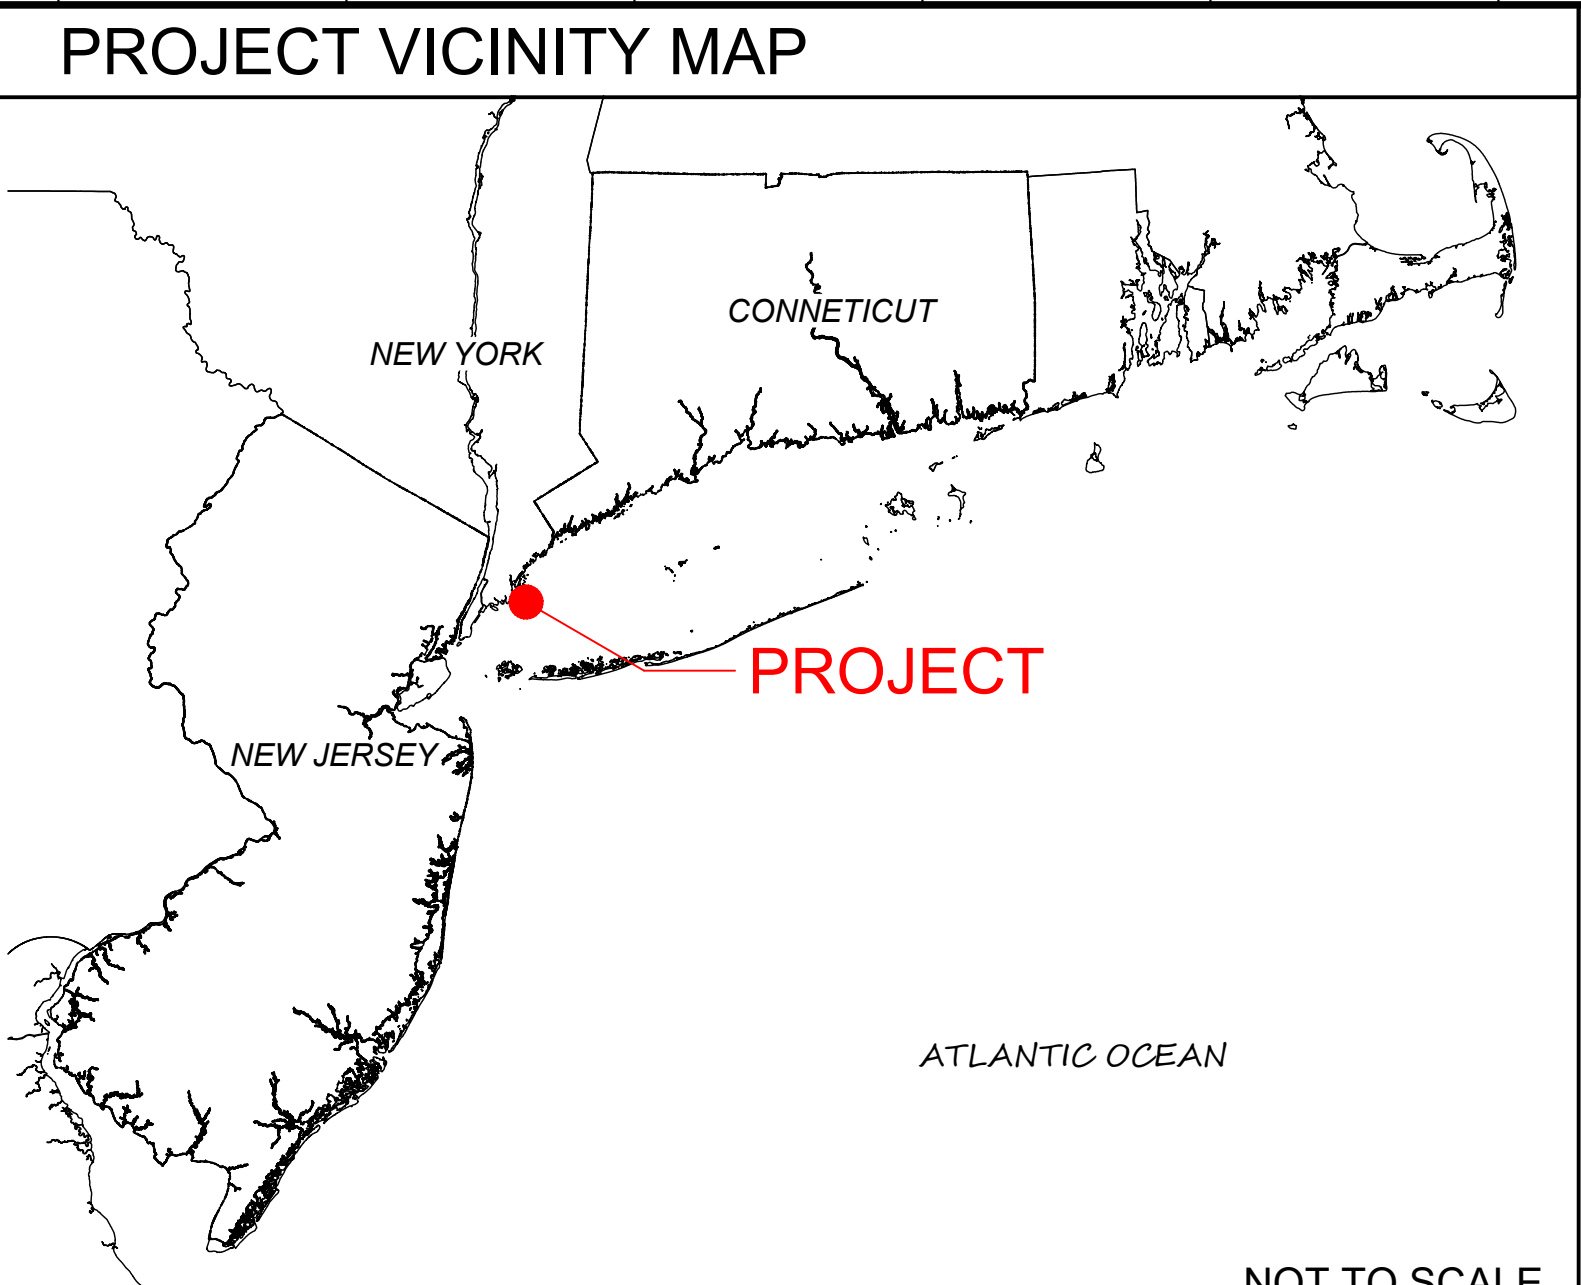


LOCAL NOAA CHART NO. 12366 (Last Update: 2024)

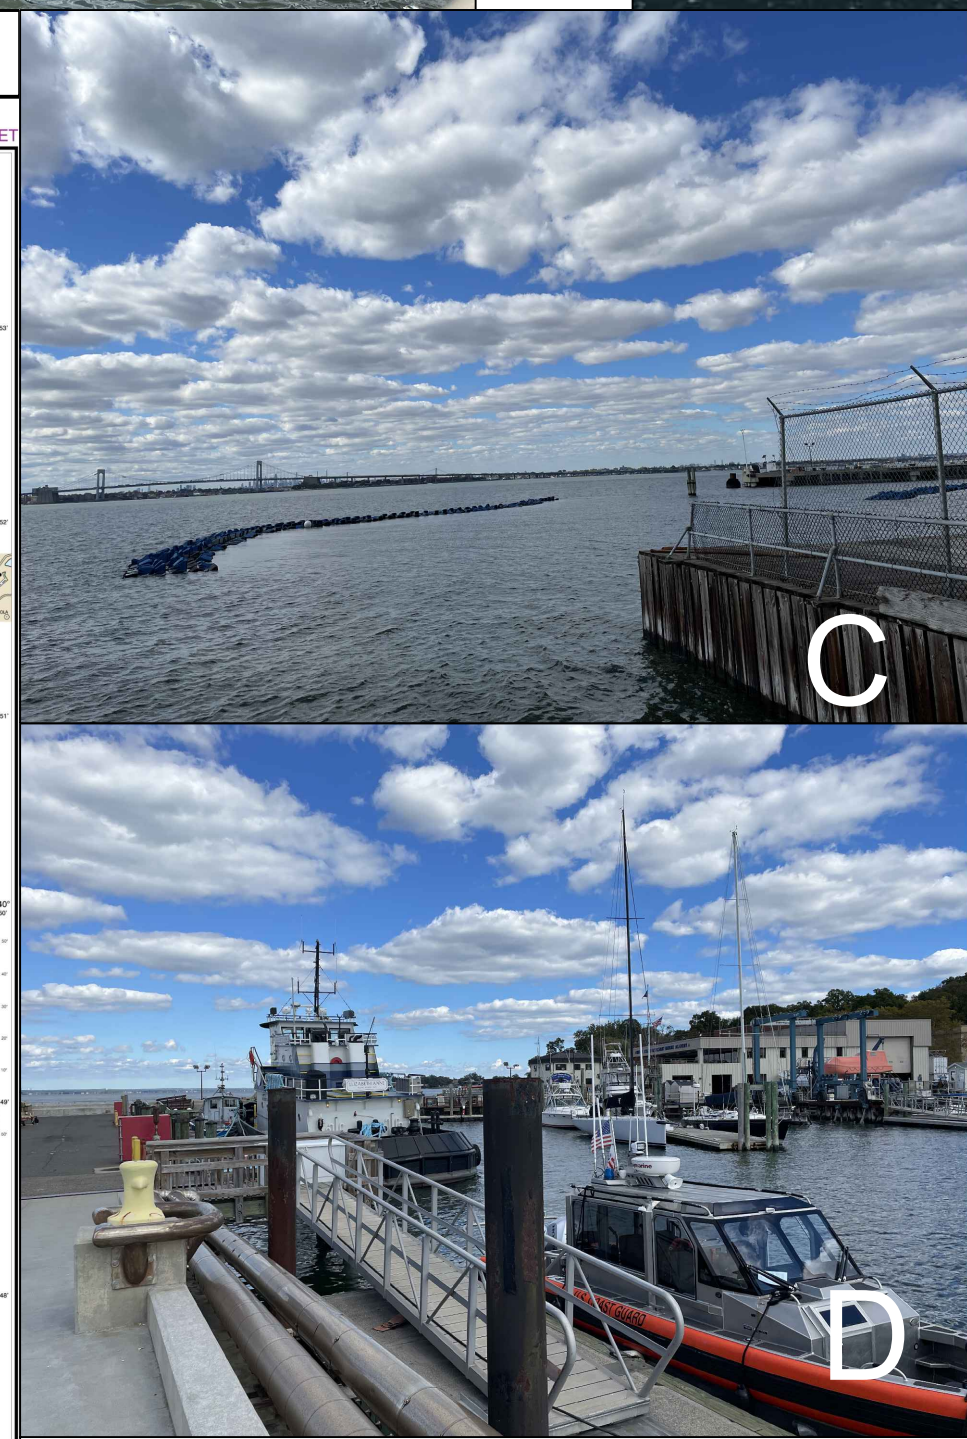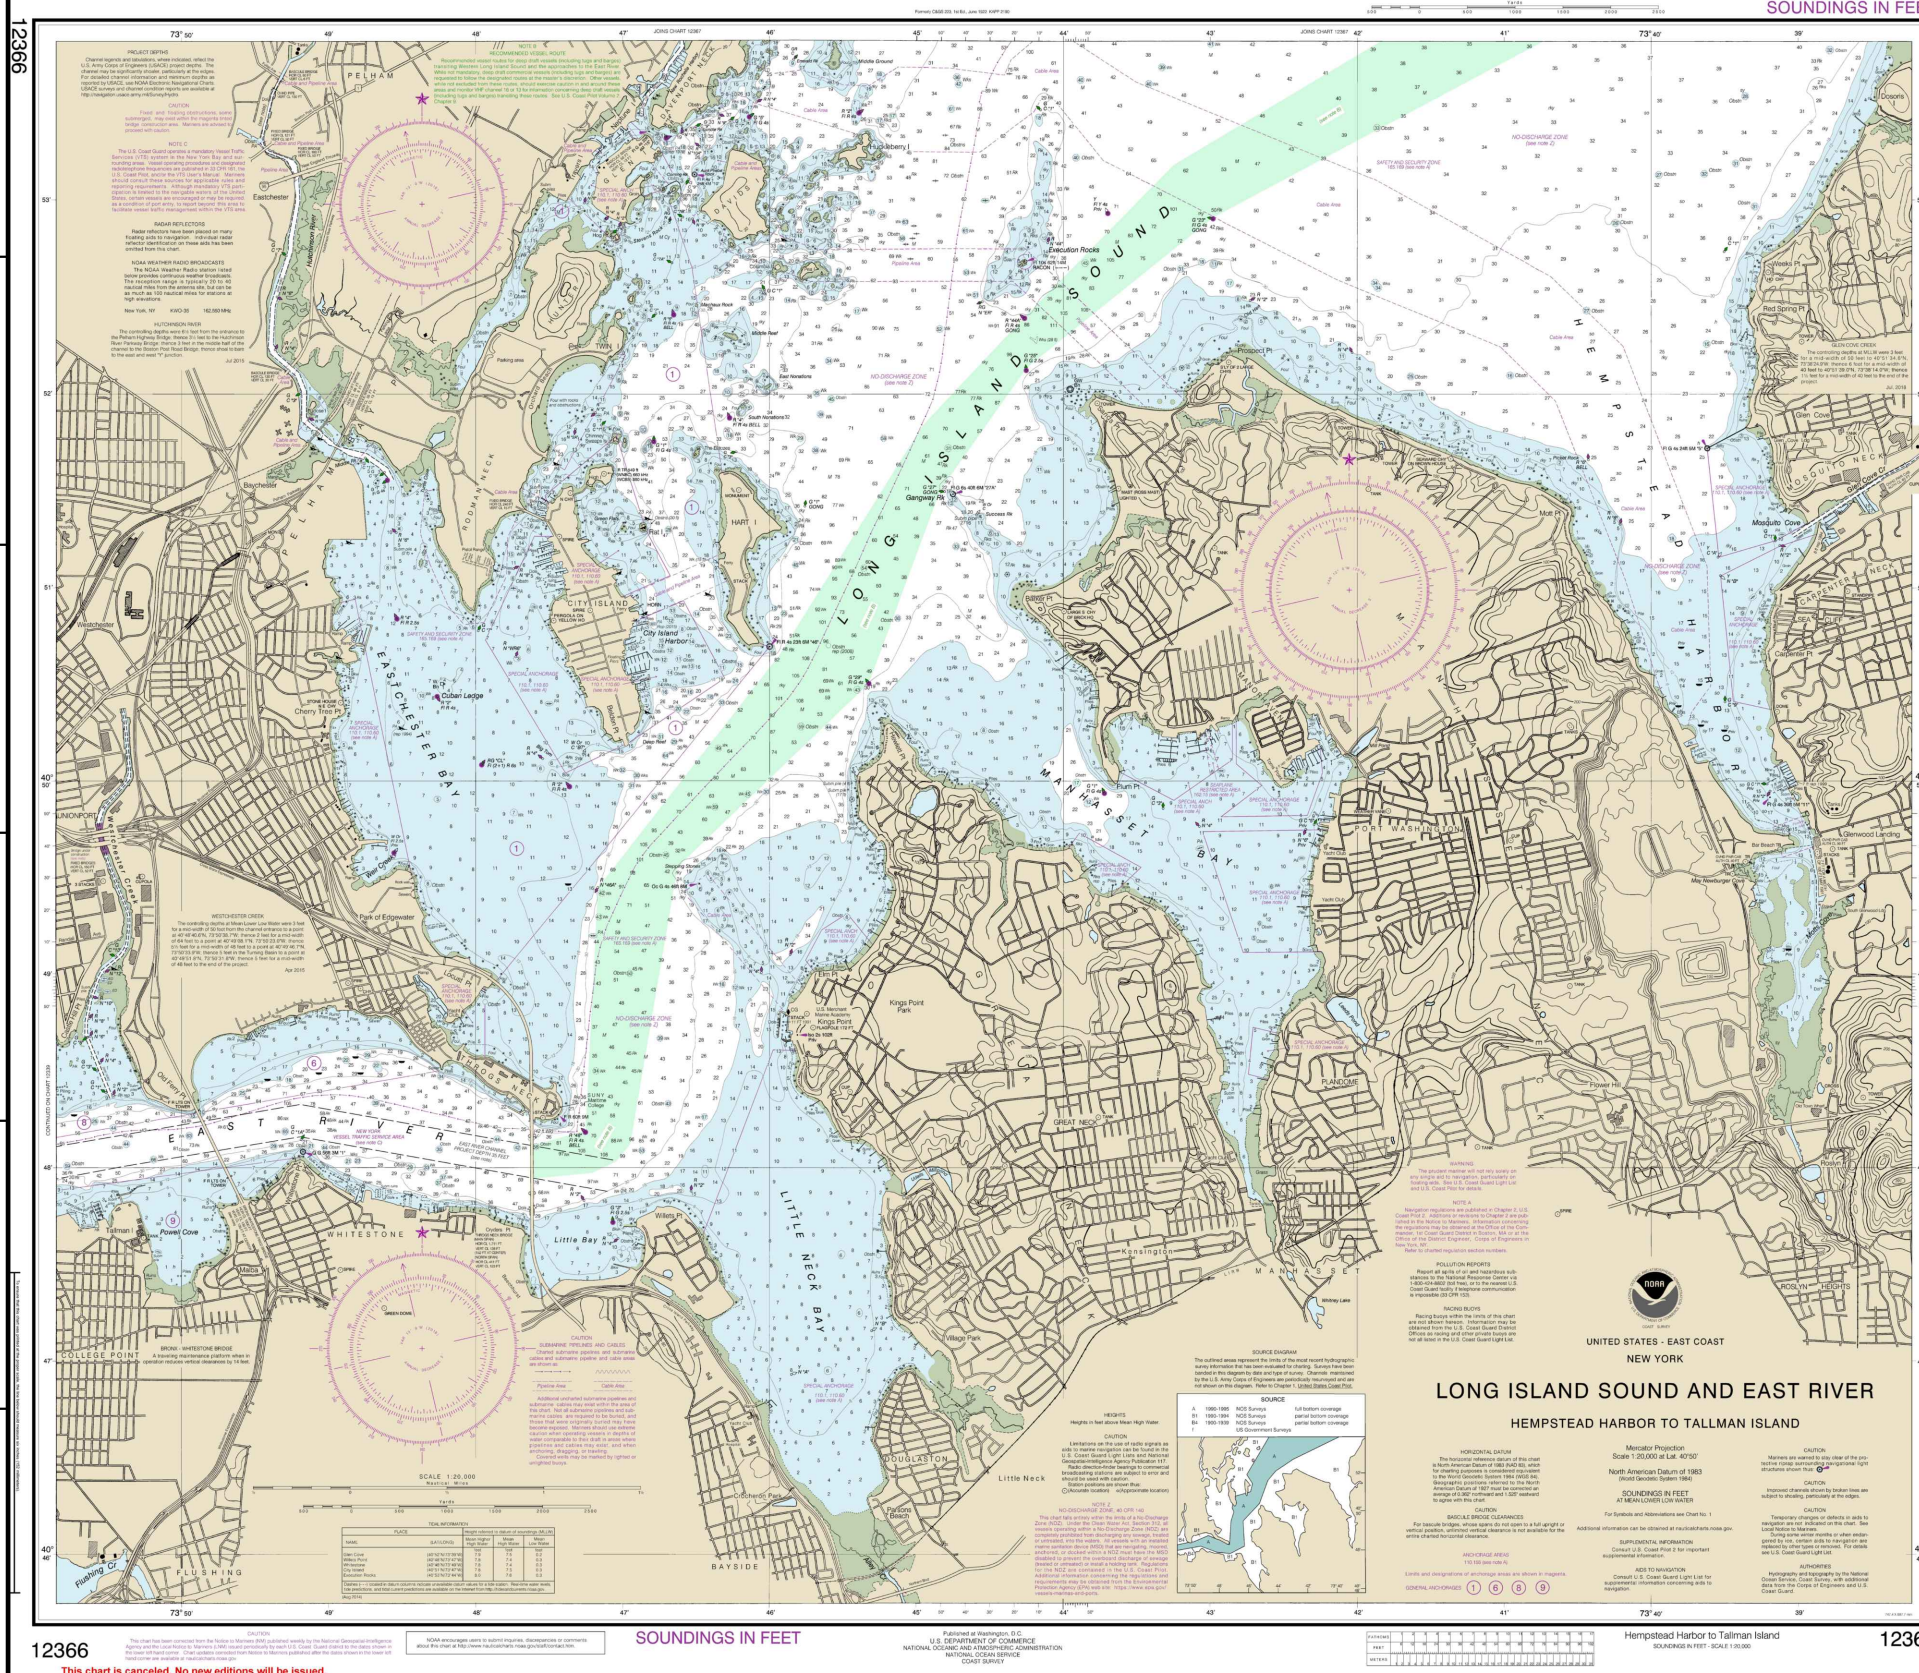

NOAA ELECTRONIC CHARTS (ENC)
CHART: US5NYCFJ
DOWNLOAD AT:
<https://www.charts.noaa.gov/InteractiveCatalog/nrmc.shtml>


PROJECT SITE PLAN

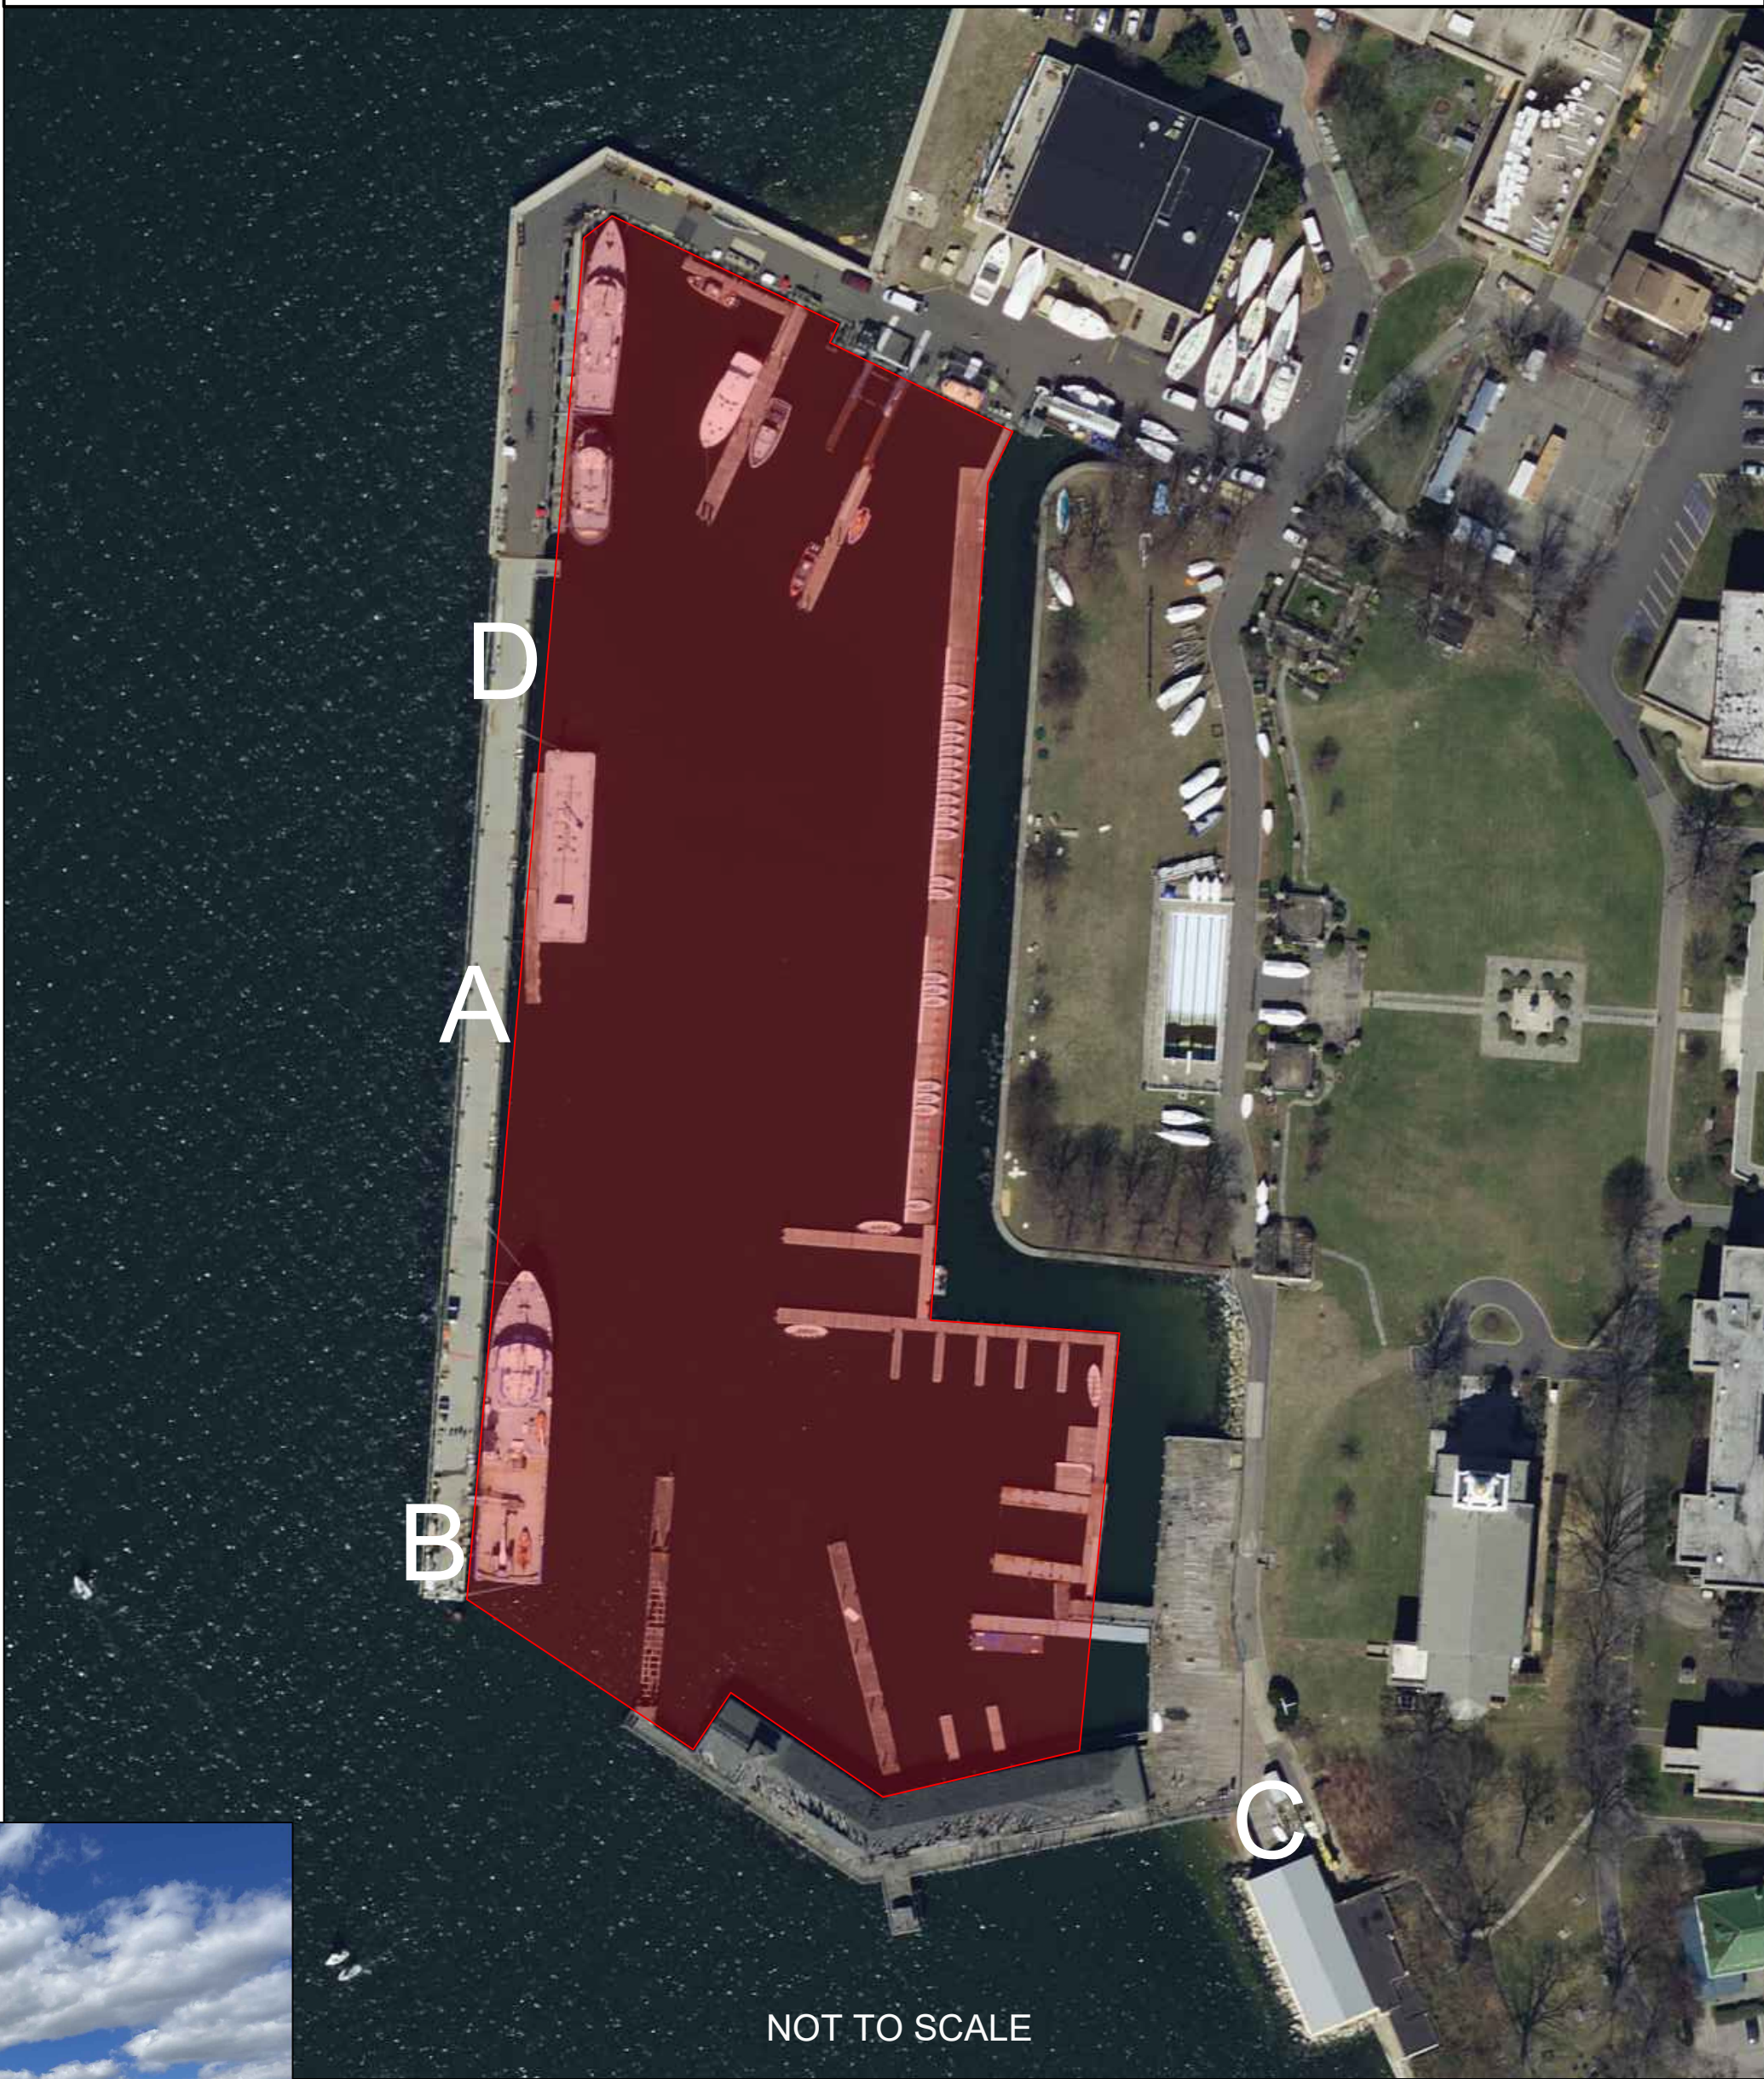

PROJECT NOTES

-THE INFORMATION DEPICTED ON THIS MAP REPRESENTS THE RESULTS OF SURVEYS MADE ON THE DATES INDICATED AND CAN ONLY BE CONSIDERED AS THE GENERAL CONDITIONS EXISTING AT THAT TIME.
-THE SOUNDINGS ON THIS MAP MEET EM 1110-2-1003 ACCURACY STANDARDS.
-THIS MAP IS CEPD COMPLIANT IN ACCORDANCE WITH ER 1110-2-8160 AND EM 1110-2-8056.
-COORDINATES REFER TO US STATE PLANE COORDINATE SYSTEM NAD 1983, LONG ISLAND LAMBERT - ZONE 3104, US SURVEY FEET.
-SOUNDINGS ON THIS MAP REFER TO THE PLANE OF MEAN LOWER LOW WATER (MLLW) [EPOCH 1983-2001].
-MEAN LOWER LOW WATER IS 4.1 FEET BELOW NAVD88 AS DETERMINED USING VDUTUM (VER. 4.6.1).
-SOUNDINGS DEPICTED ON THIS MAP ARE BASED ON A 3' x 3' MEDIAN CELL, SORTED TO A 10' INTERVAL.
-CONTOURS ON THIS MAP WERE GENERATED USING THE 3 x 3 DATA SET.
-THE DATA DEPICTED ON THIS MAP SHOULD NOT BE USED FOR VOLUME CALCULATION PURPOSES.
-AERIAL IMAGERY PROVIDED BY NYGIN 2023 AND IS FOR ORIENTATION PURPOSES ONLY.
-THE PLANIMETRICS DEPICTED ON THIS MAP ARE FOR ORIENTATION PURPOSES ONLY.
-THIS SURVEY WAS PERFORMED USING REAL TIME KINEMATIC GPS FROM STATION "851 6945 TIDAL 5".
-THE CONTRACTOR SHALL BE RESPONSIBLE FOR ANY DAMAGE CAUSED BY THEM ON ANY STRUCTURES AND UTILITIES OR ANY OTHER PROPERTY ADJACENT TO THE DREDGING AREA, INCLUDING ANY EXISTING FLOATING DOCKS AND PILES THAT MAY BE WITHIN THE DREDGING FOOTPRINT.



PROJECT LEGEND

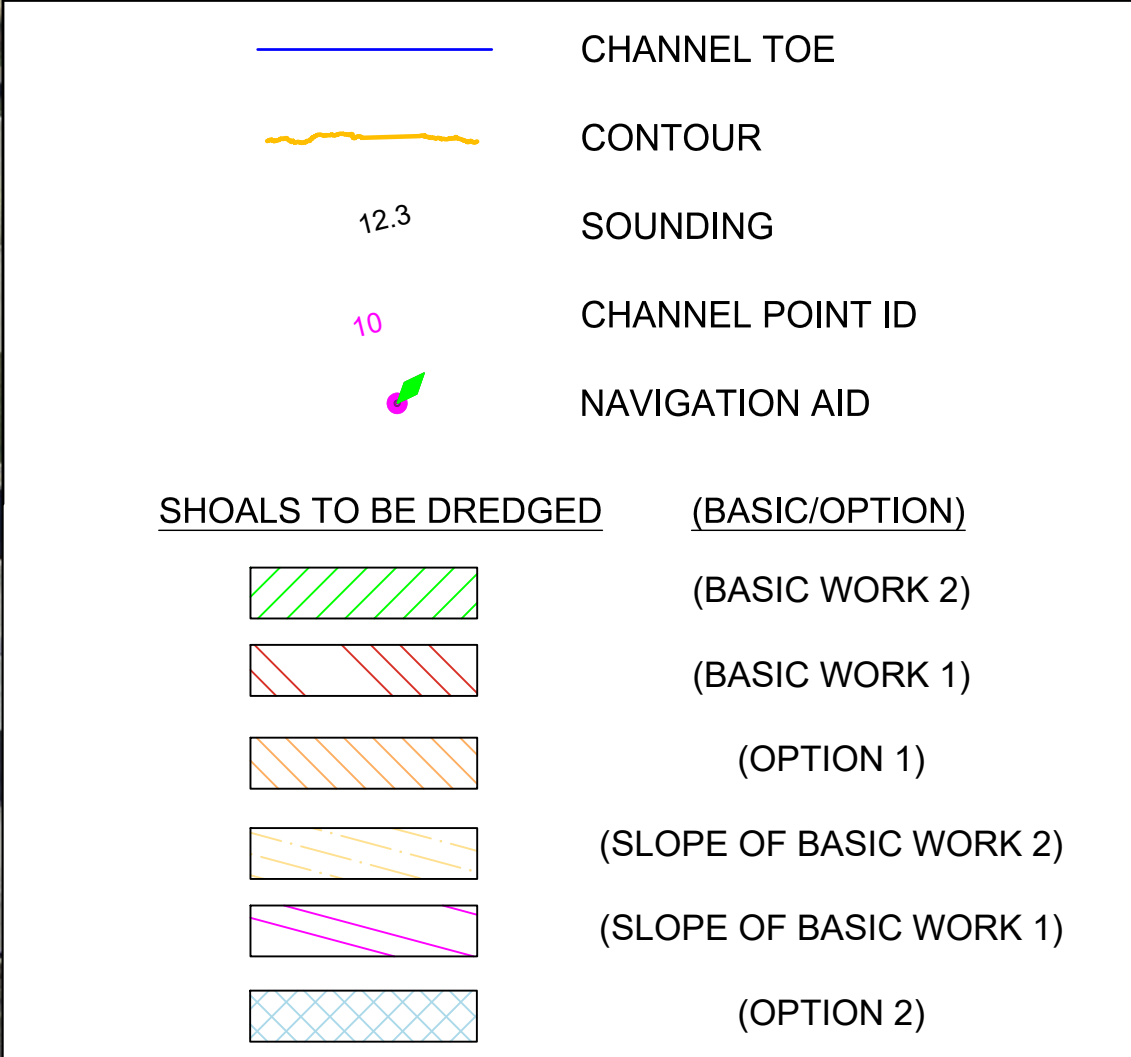

PROJECT SITE PLAN LEGEND

DREDGE AREA
A: MALLORY PIER
B: BREAKWATER STRUCTURE
C: BREAKWATER STRUCTURE ALTERNATE VIEW
D: FLOATING DOCKS & BOAT TRAVEL LIFT

TYPICAL DREDGING CROSS SECTION

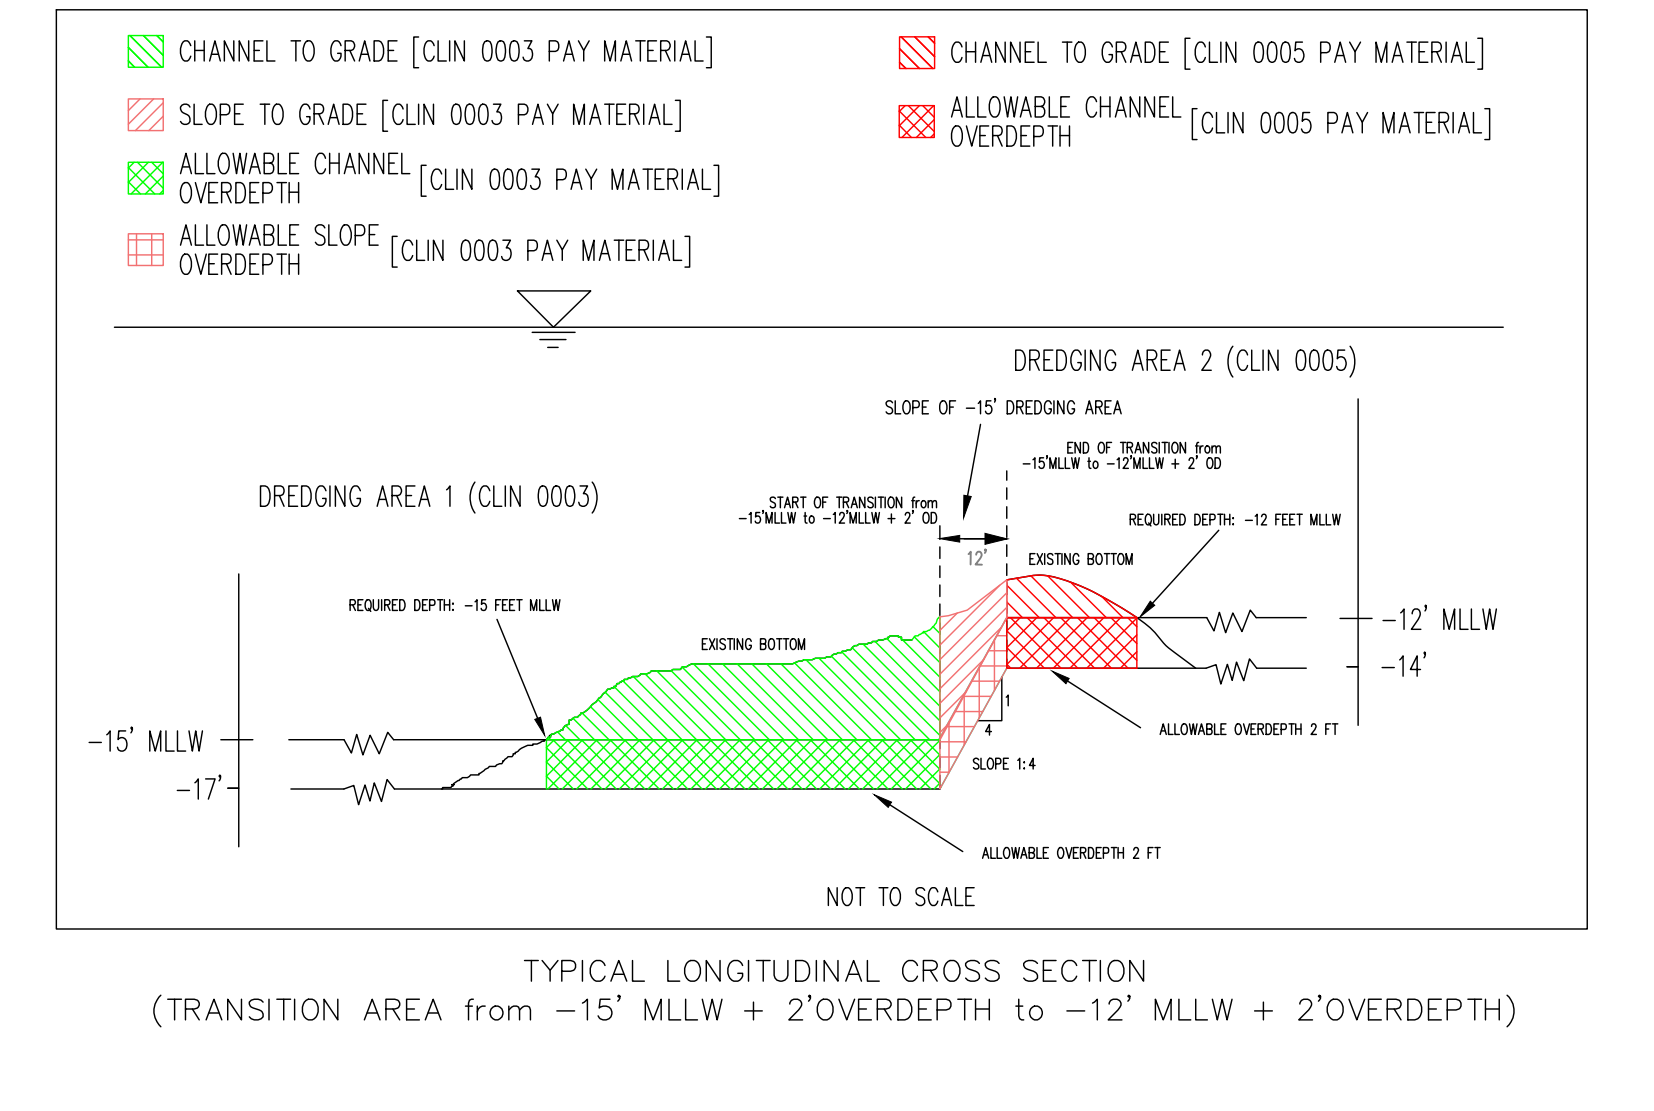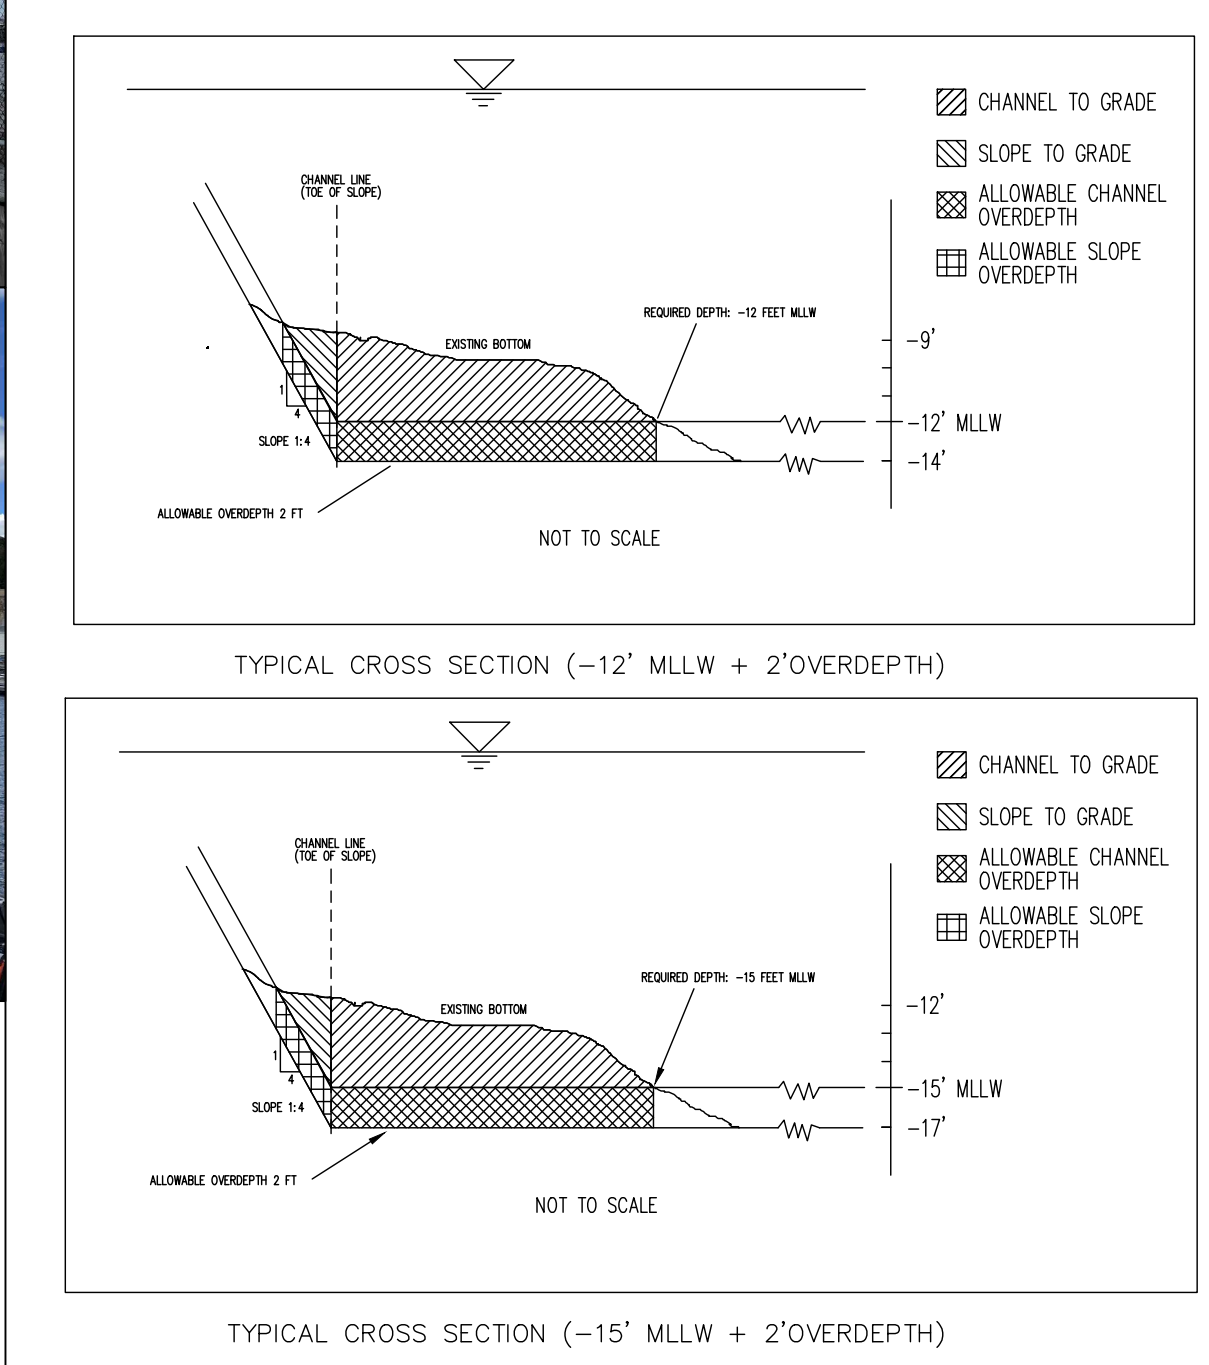

ISSUE DATE:	DATE
DESIGNED BY:	MARK
CHECKED BY:	DESCRIPTION
APPROVED BY:	MARK
ISSUE DATE:	DATE
DESIGNED BY:	MARK
CHECKED BY:	DESCRIPTION
APPROVED BY:	MARK

U.S. ARMY CORPS OF ENGINEERS
DEPARTMENT OF THE ARMY
NEW YORK DISTRICT
NEW YORK, NEW YORK 10278


OPERATIONS DIVISION
TECHNICAL SUPPORT SECTION
CENAN-OP-ST

MAINTENANCE DREDGING
HAGUE BASIN
U.S. MERCHANT MARINE ACADEMY
KINGS POINT, NEW YORK

PROJECT SITE PLAN & NOTES

SHEET ID
GI-101
2 OF 3

SOLICITATION PLANS

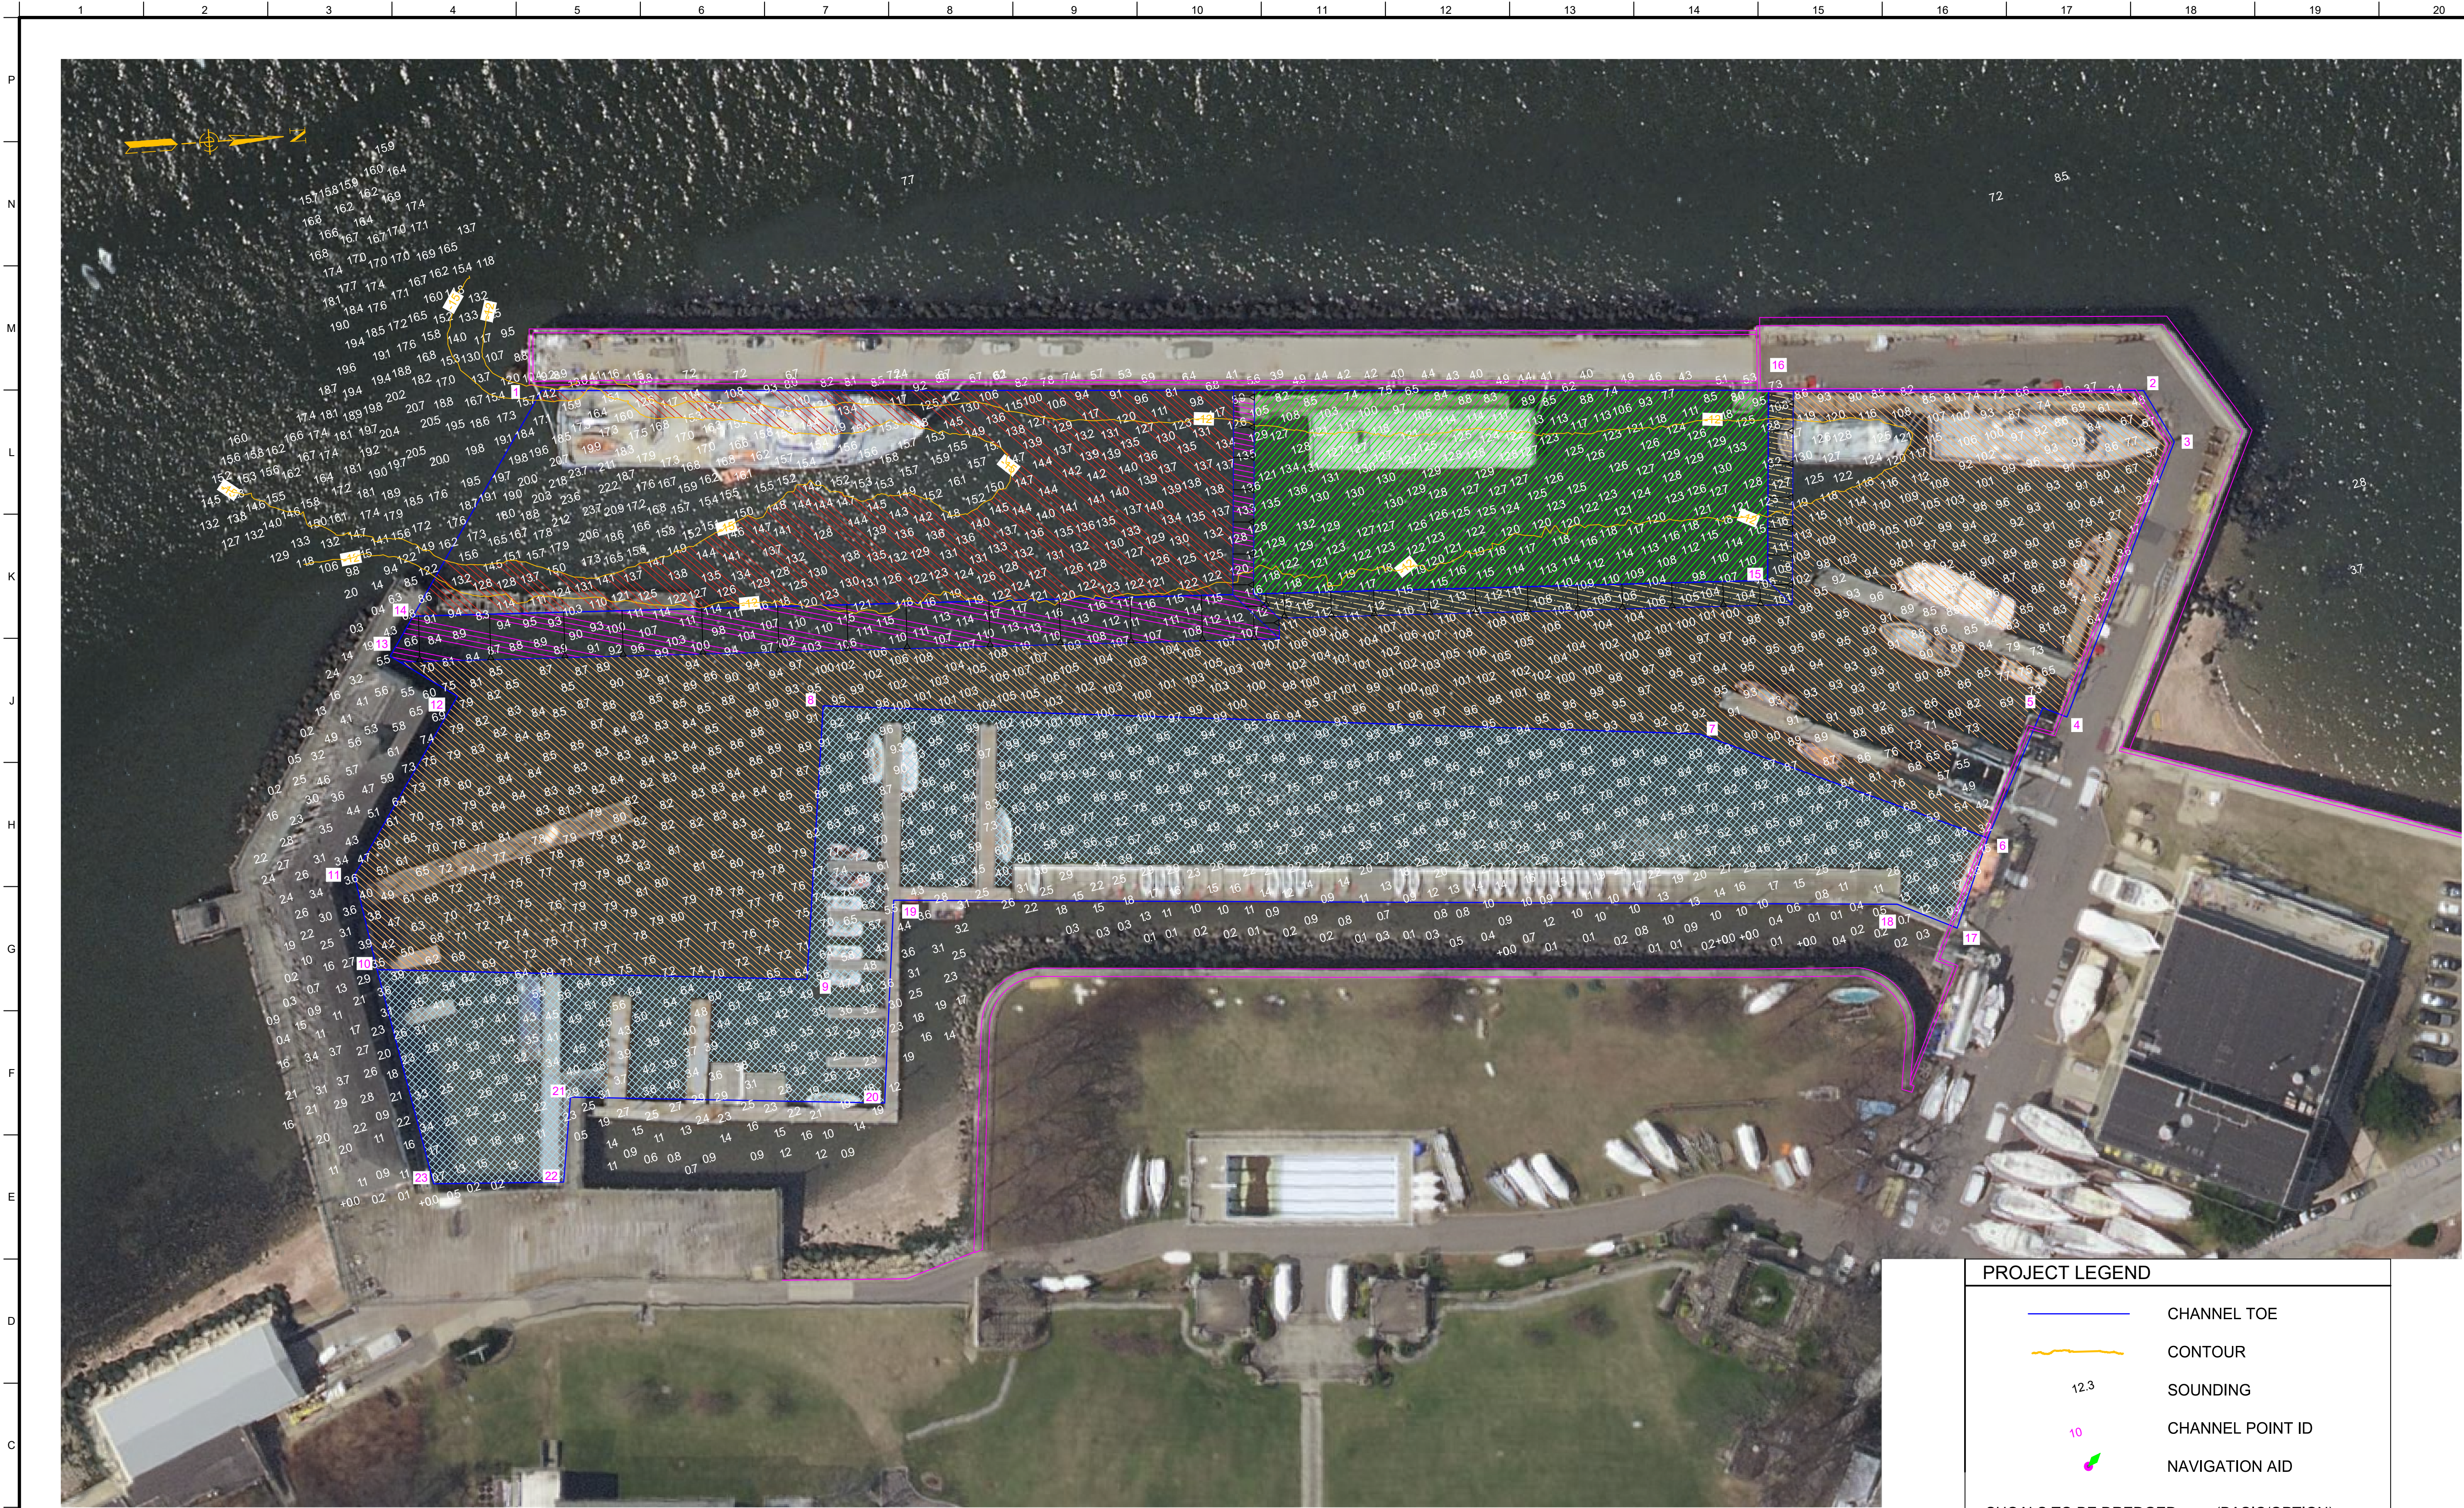

04080Feet

NSRS BENCHMARK

BENCHMARK: 851 6945 TIDAL 5 (PID-DE7792)
ELEVATION: 10.88'

LOCAL CONTROL

BENCHMARK: 851 6945 D
ELEVATION: 11.66'

PROJECT SPECIFIC NOTES LOCATED ON SHEET GI-101

PROJECT LEGEND

CHANNEL TOE

CONTOUR

SOUNDING

CHANNEL POINT ID

NAVIGATION AID

SHOALS TO BE DREDGED

(BASIC/OPTION)

(BASIC WORK 2)

(BASIC WORK 1)

(OPTION 1)

(SLOPE OF BASIC WORK 2)

(SLOPE OF BASIC WORK 1)

(OPTION 2)

MAINTENANCE DREDGING
HAGUE BASIN
U.S. MERCHANT MARINE ACADEMY
KINGS POINT, NEW YORK

DREDGING AREA & SOUNDING MAP

DESIGNED BY:
DAVID M. GREENE
DRAWN BY:
DAVID M. GREENE
CHECKED BY:
MICHAEL J. LEEBACK
SUBMITTED BY:
MICHAEL J. LEEBACK

U.S. ARMY CORPS OF ENGINEERS
DEPARTMENT OF THE ARMY
NEW YORK DISTRICT
NEW YORK, NEW YORK 10278

OPERATIONS DIVISION
OPERATIONS SUPPORT BRANCH
TECHNICAL SUPPORT SECTION
CENANOP-ST

ISSUE DATE:
MARCH 2026
SOLICITATION NO.:
W17ZDS26-BA011
CONTRACT NO.:
W17ZDS26-CDDXX
SCALE:
ONE INCH = 40 FEET

ANS/D

MARK

DESCRIPTION

DATE

SHEET ID
C-101
3 OF 3

SOLICITATION PLANS