




REMOVE AND REPLACE PUBLIC ADDRESS SYSTEM


WEST PALM BEACH VAMC
7305 NORTH MILITARY TRAIL
WEST PALM BEACH FL, 33410-6400

VA PROJECT #: 548-22-100

PROJECT SITE MAP

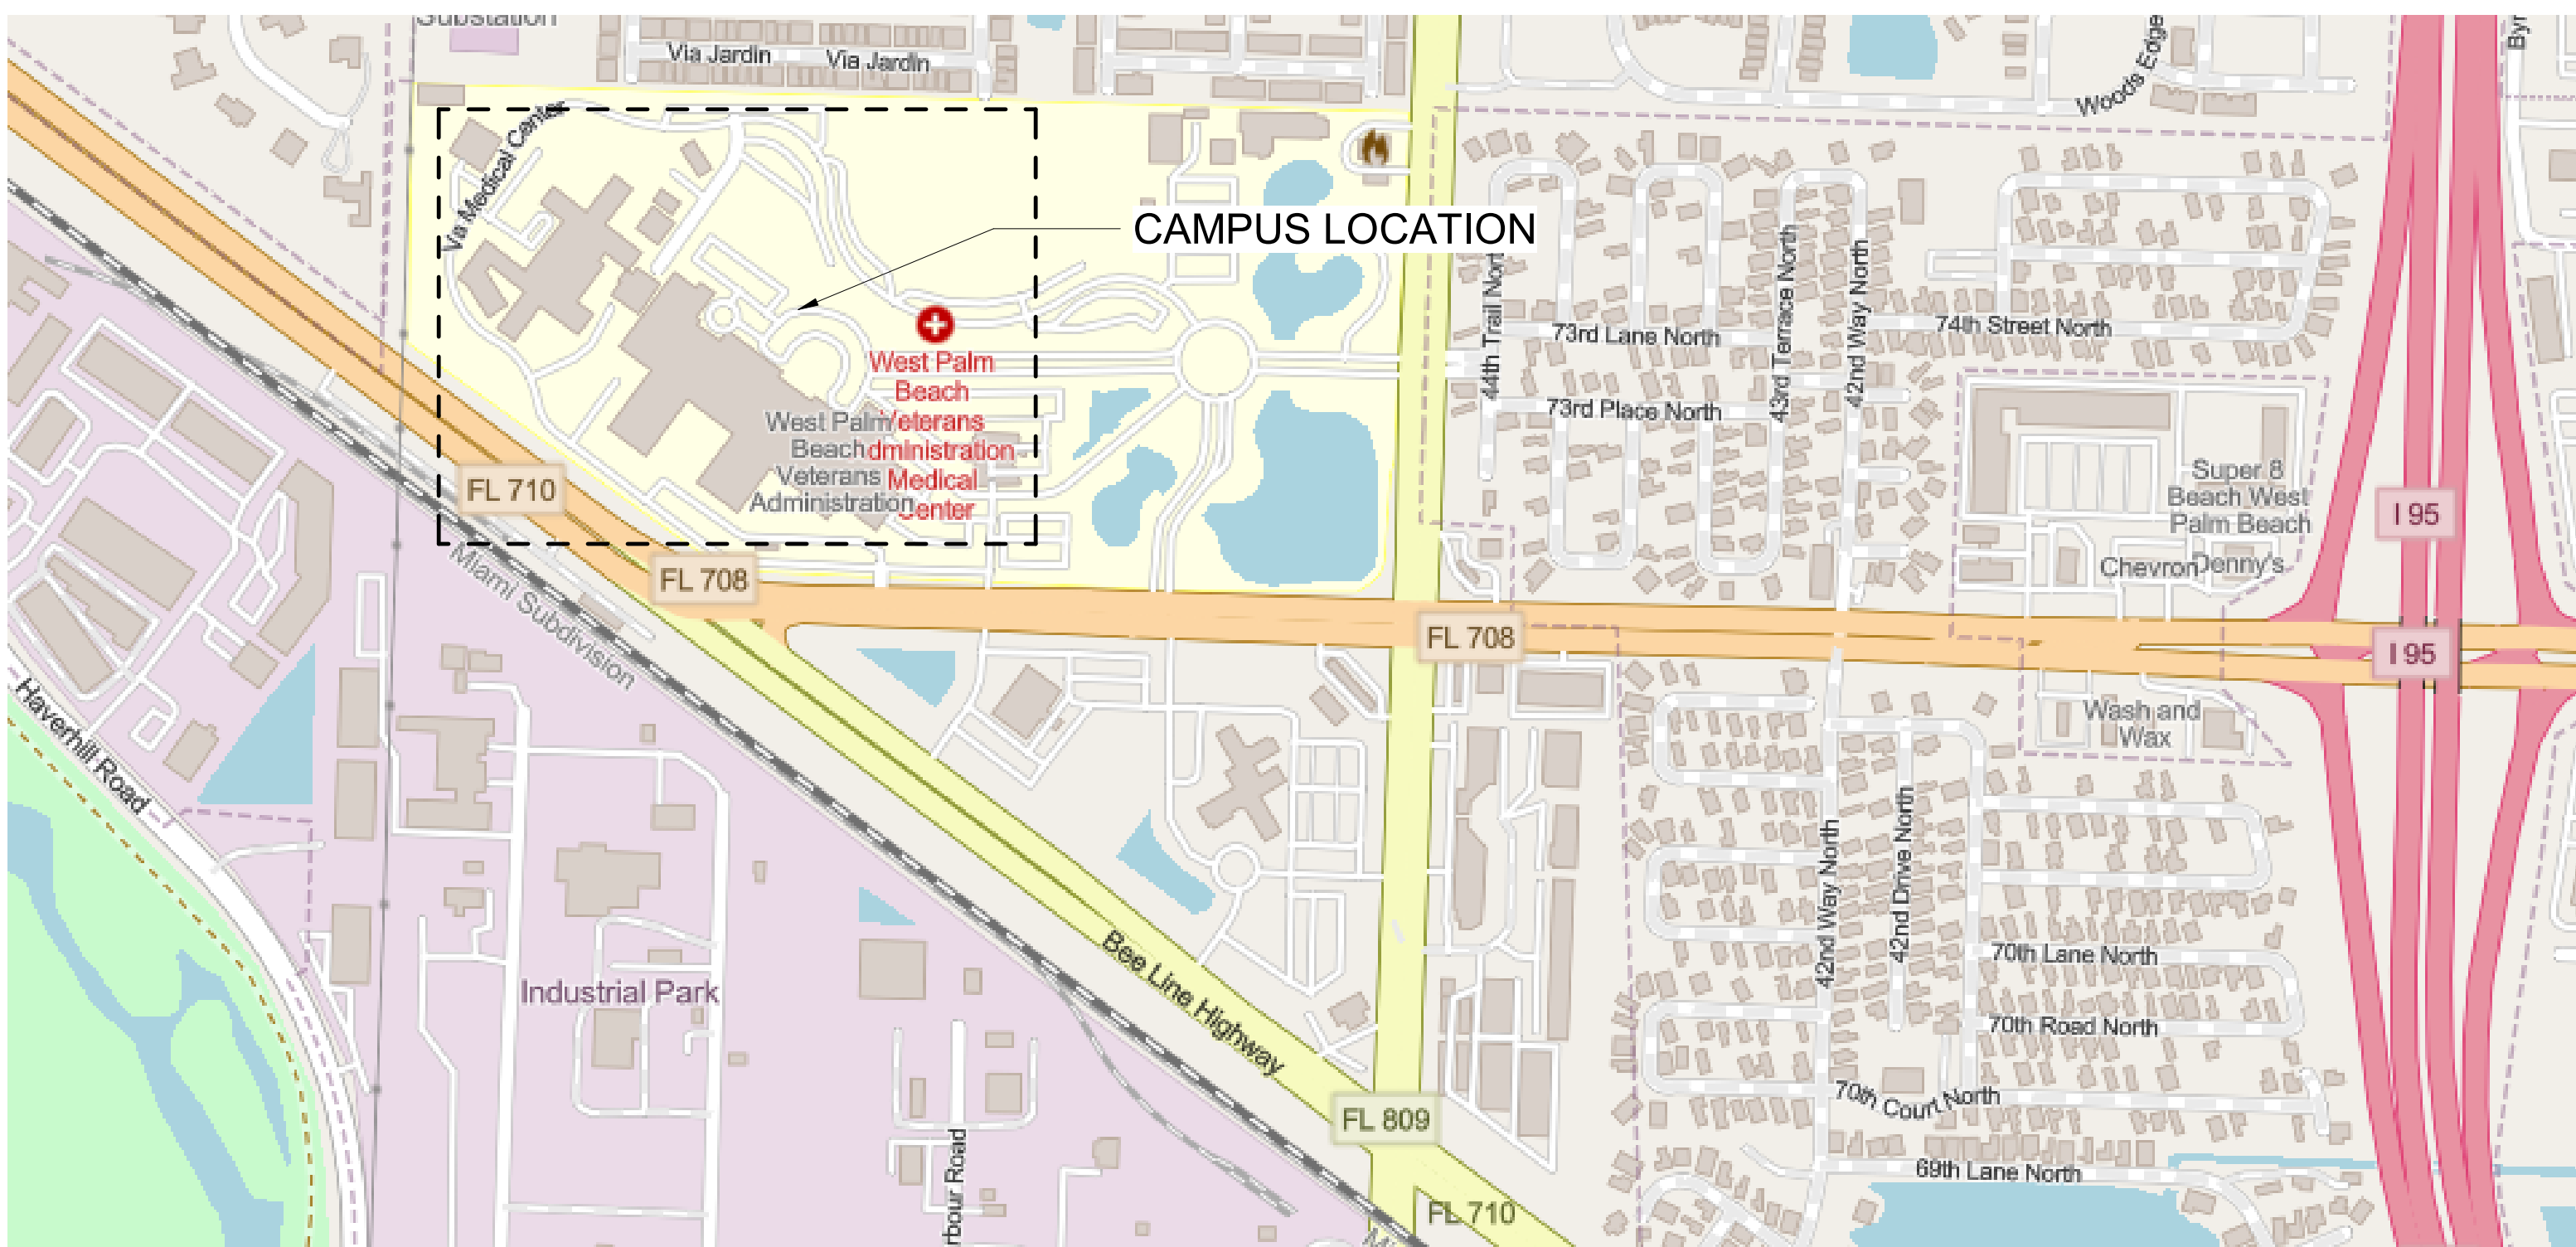

PROJECT LOCATION MAP

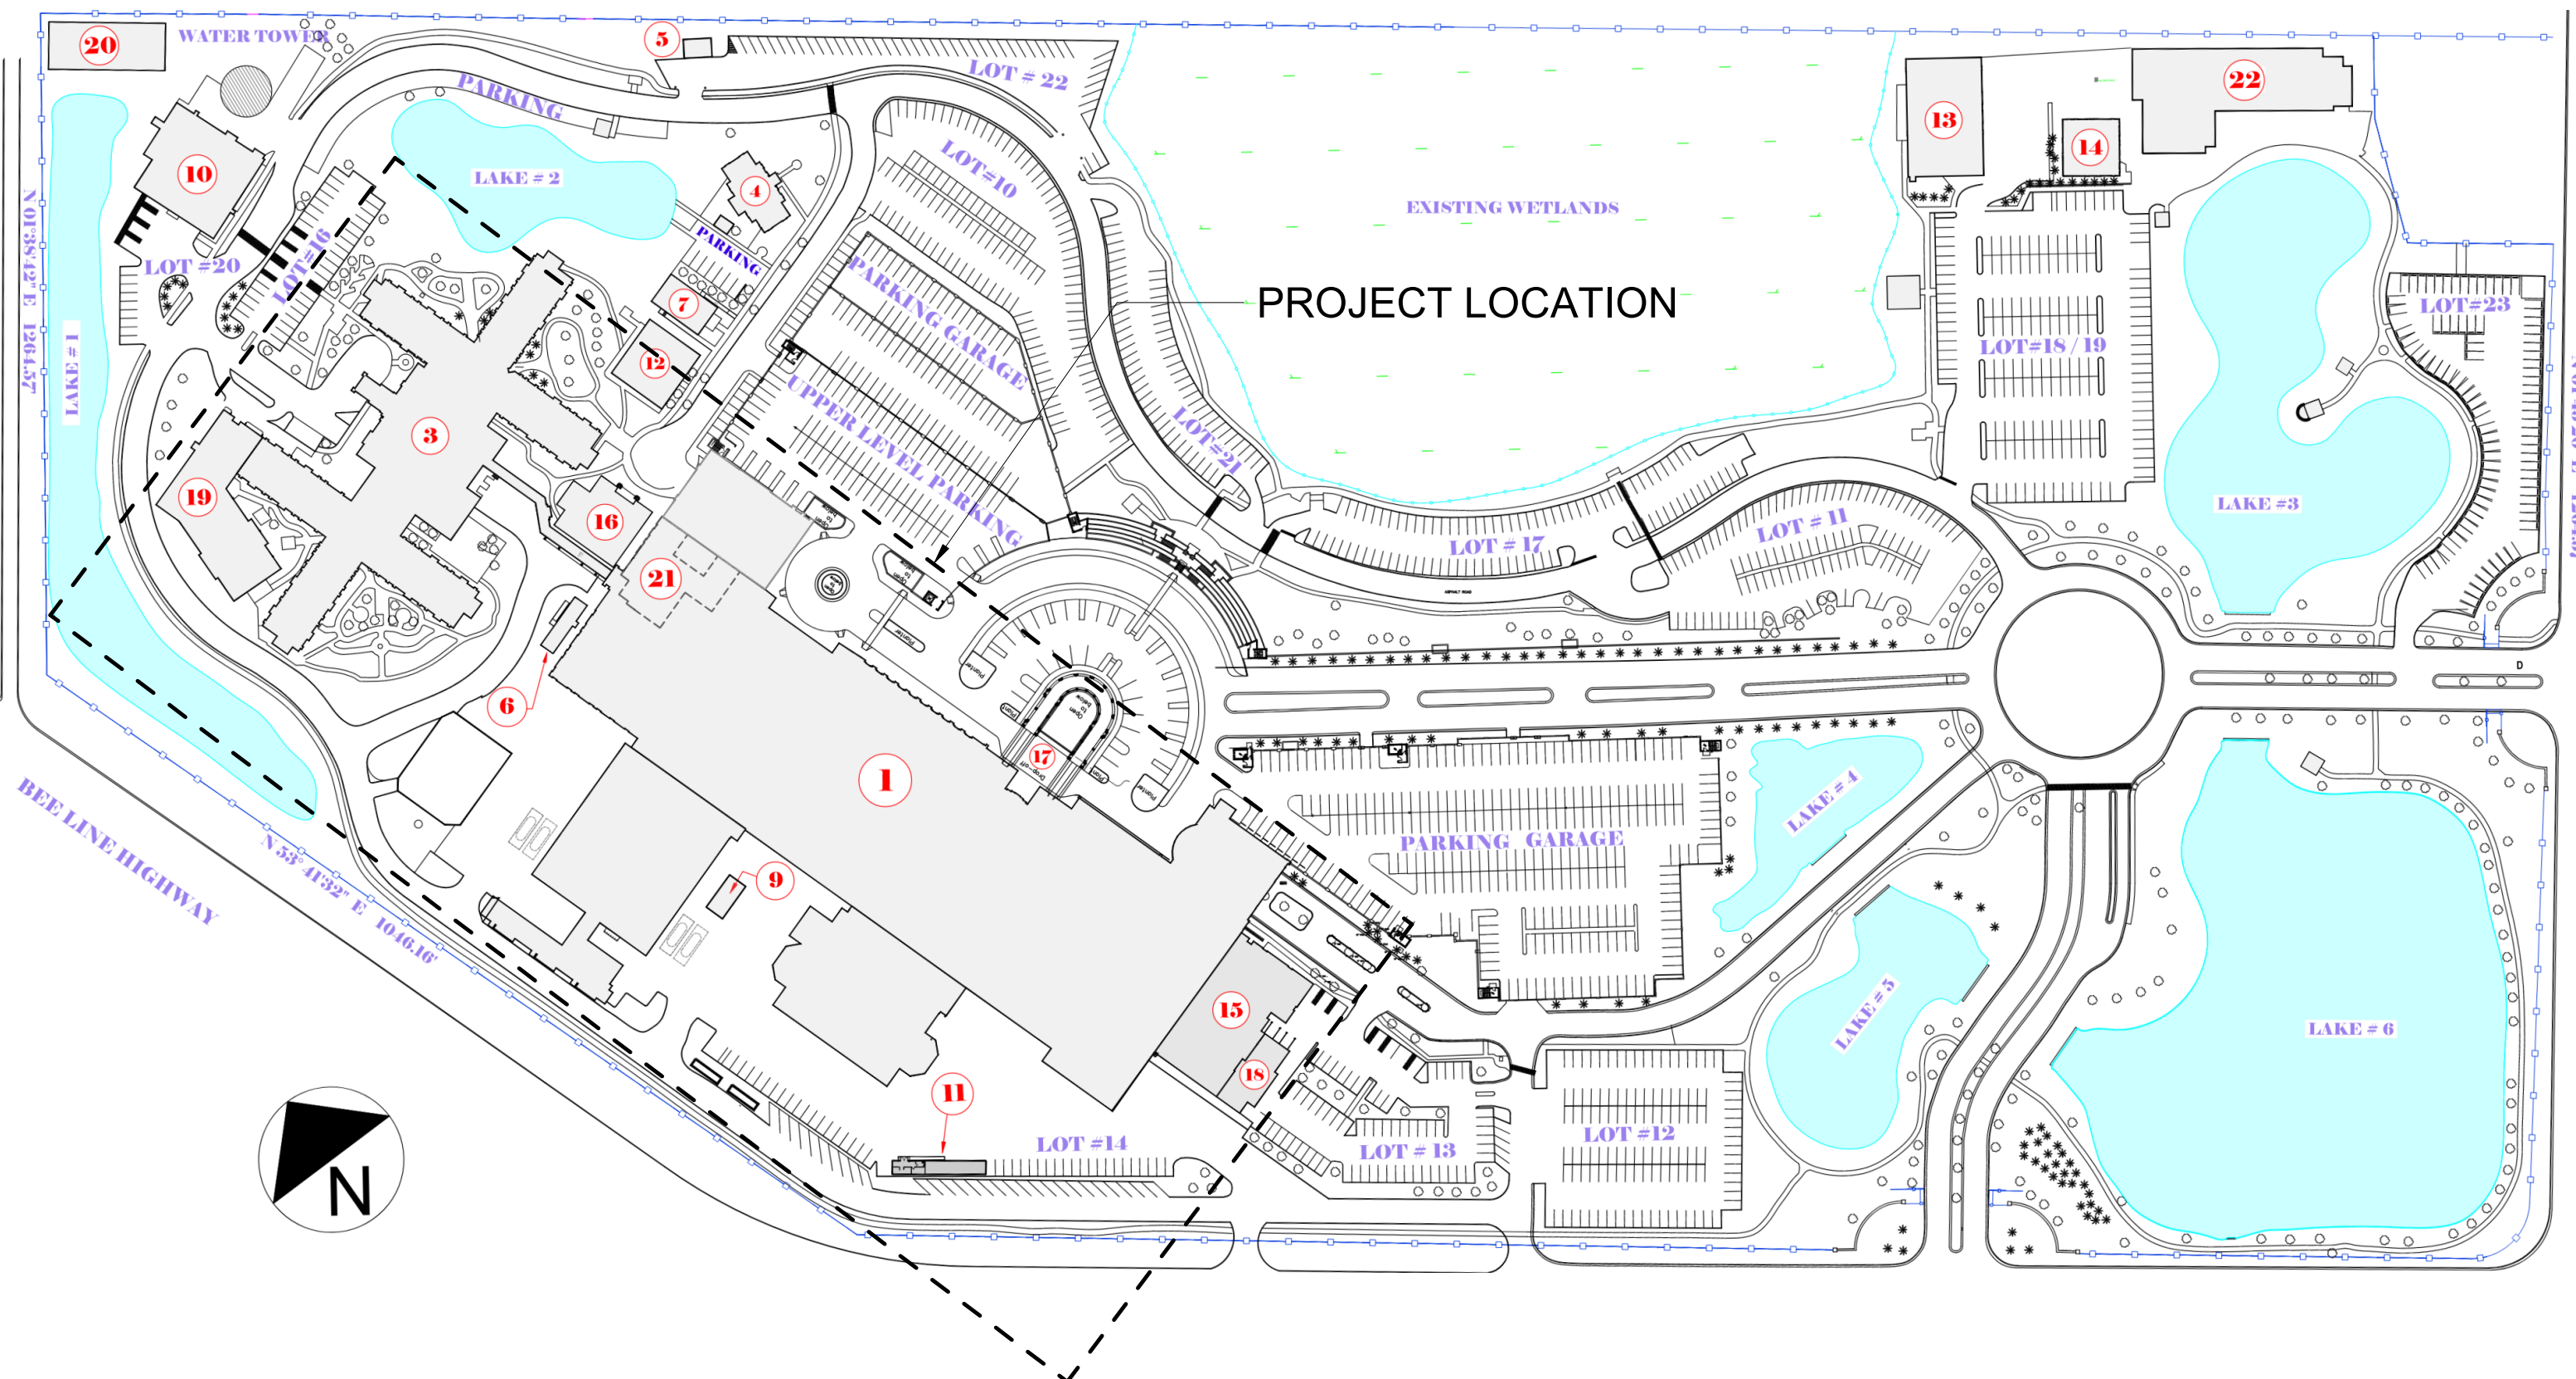

DRAWING LIST


GENERAL			
G-001	COVER	1	4
G-002	GENERAL INFORMATION	2	4
G-003	ICRA INFORMATION AND DETAILS	3	4
G-004	PRE-CONSTRUCTION RISK ASSESSMENT FORMS	4	4
TECHNOLOGY			
T-001	TECHNOLOGY GENERAL NOTES, SYMBOL LEGEND, AND ABBREVIATIONS	1	32
T-101	BASEMENT FLOOR SE PAMNS	2	32
T-102	BASEMENT FLOOR CENT PAMNS	3	32
T-103	BASEMENT FLOOR NW PAMNS	4	32
T-104	BASEMENT FLOOR E PAMNS	5	32
T-105	CLC NE PAMNS	6	32
T-106	CLC SW PAMNS	7	32
T-111	FIRST FLOOR SE PAMNS	8	32
T-112	FIRST FLOOR CENT PAMNS	9	32
T-113	FIRST FLOOR NW PAMNS	10	32
T-114	FIRST FLOOR E PAMNS	11	32
T-115	FIRST FLOOR S PAMNS	12	32
T-121	SECOND FLOOR SE PAMNS	13	32
T-122	SECOND FLOOR CENT PAMNS	14	32
T-123	SECOND FLOOR NW PAMNS	15	32
T-131	THIRD FLOOR SE PAMNS	16	32
T-132	THIRD FLOOR CENT PAMNS	17	32
T-133	THIRD FLOOR NW PAMNS	18	32
T-141	FOURTH FLOOR SE PAMNS	19	32
T-142	FOURTH FLOOR CENT PAMNS	20	32
T-143	FOURTH FLOOR NW PAMNS	21	32
T-151	FIFTH FLOOR PAMNS SE	22	32
T-152	FIFTH FLOOR PAMNS NW	23	32
T-161	SIXTH FLOOR PAMNS	24	32
T-171	SEVENTH FLOOR PAMNS	25	32
T-181	EIGHTH FLOOR PAMNS	26	32
T-191	NINTH FLOOR PAMNS	27	32
T-192	TENTH FLOOR PAMNS	28	32
T-401	TECHNOLOGY ENLARGEMENTS	29	32
T-402	TECHNOLOGY ENLARGEMENTS	30	32
T-501	TECHNOLOGY DETAILS	31	32
T-601	PAMNS RISER DIAGRAM	32	32

PROJECT IMAGE




FULLY SPRINKLERED
100% CONSTRUCTION DOCUMENTS


CONSULTANTS:			PROJECT MANAGER		Office of Construction and Facilities Management		Drawing Title COVER		Project Title REMOVE AND REPLACE PUBLIC ADDRESS SYSTEM		VA PROJECT NUMBER 548-22-100	
			Headquarters: Apogee Consulting Group, P.A. 1151 Kildaire Farm Road, Suite 120 Cary, North Carolina 27511		U.S. Department of Veterans Affairs		Location WEST PALM BEACH VAMC 7305 NORTH MILITARY TRAIL WEST PALM BEACH FL, 33410-6400		Approved		Building Number AS NOTED	
			www.acg-pa.com		919-858-7420		Date DECEMBER 14, 2022		Checked DJR		Drawing Number G-001	
							Drawn LMB				Dwg 1 of 4	

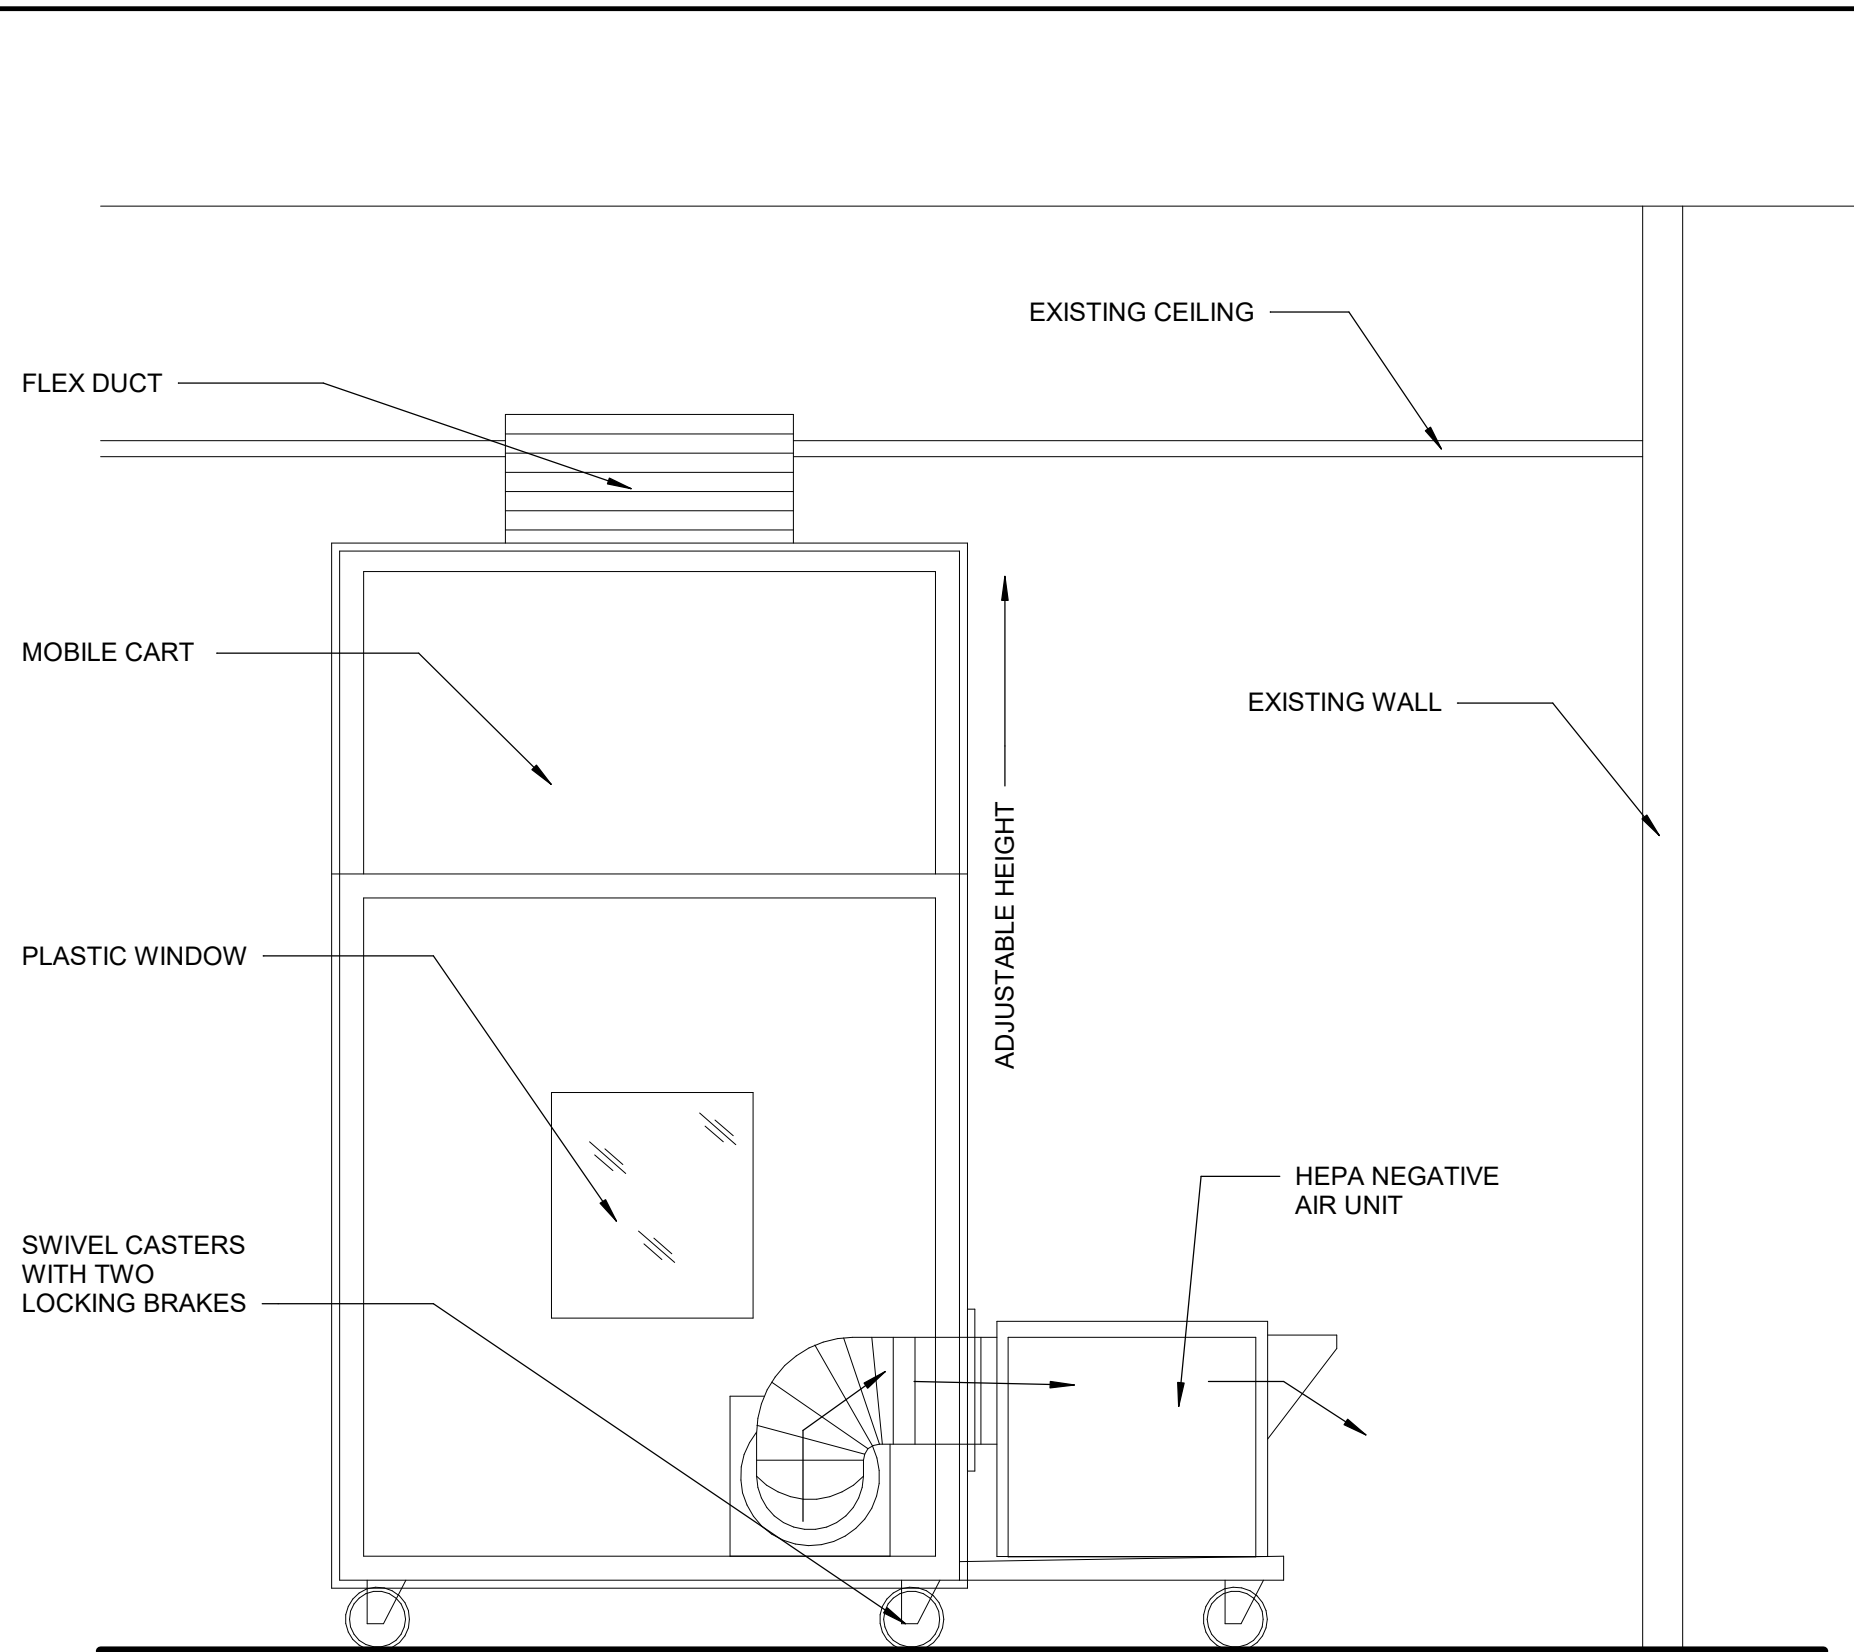

3 ICRA MOBILE CONTAINMENT CART
Scale: 1/2" = 1'-0"

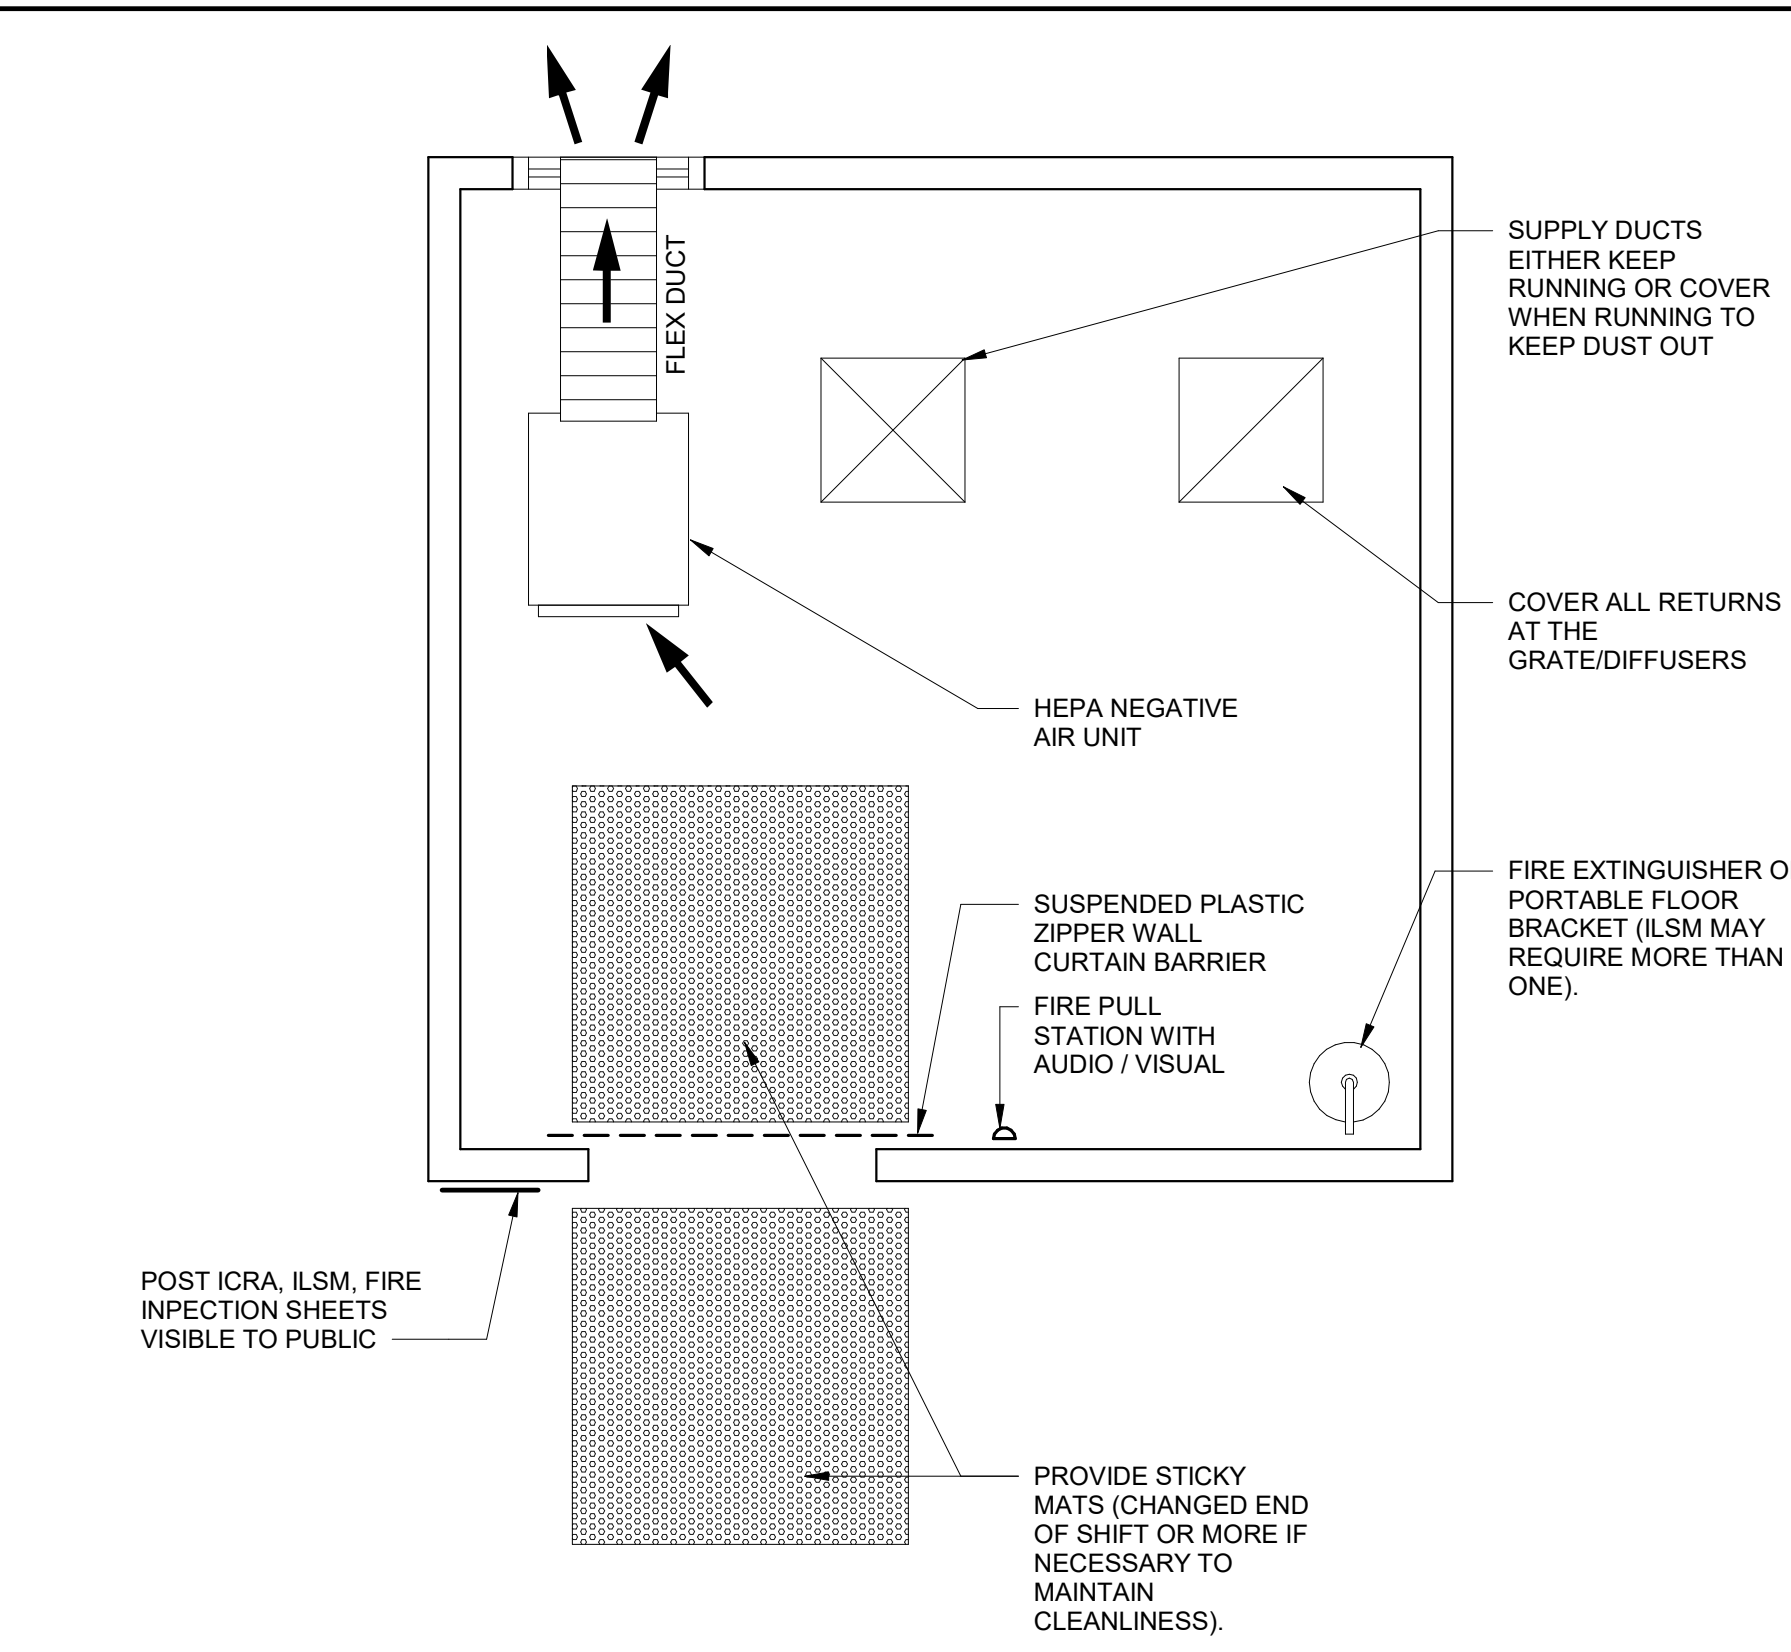


1 TYPICAL CONSTRUCTION PLAN LAYOUT
Scale: 1/2" = 1'-0"

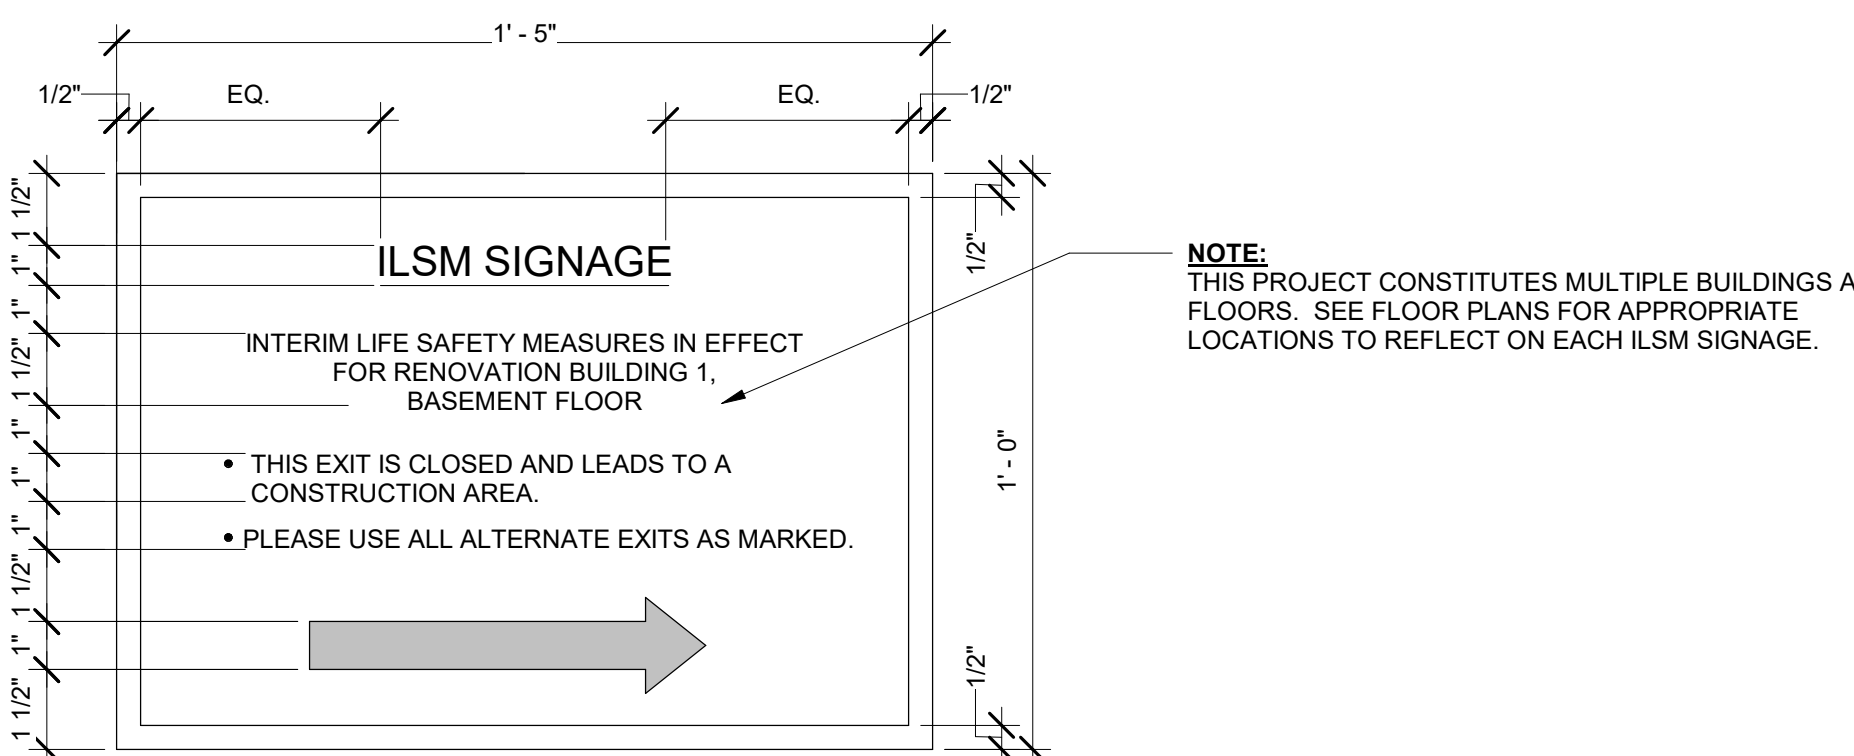


4 ILSM CONSTRUCTION EGRESS SIGNAGE
Scale: 3" = 1'-0"

ISLM TEMPORARY BARRIER TAG	
PROJECT:	
PRIME CONTRACTOR:	
SUB CONTRACTOR:	
EMERGENCY CONTACT NO.:	
BARRIER INSTALLATION DATE:	
BARRIER EXPIRATION DATE:	

NOTE: ICRA AND LIFE SAFETY FLOOR PLANS SHOW SOME SPECIFIC LOCATIONS WHERE ICRA BARRIERS ARE REQUIRED. OTHER WORK MAY REQUIRE ICRA BARRIERS, AND THESE DETAILS PROVIDE TYPICAL GUIDANCE FOR CONSTRUCTING ICRA BARRIERS.

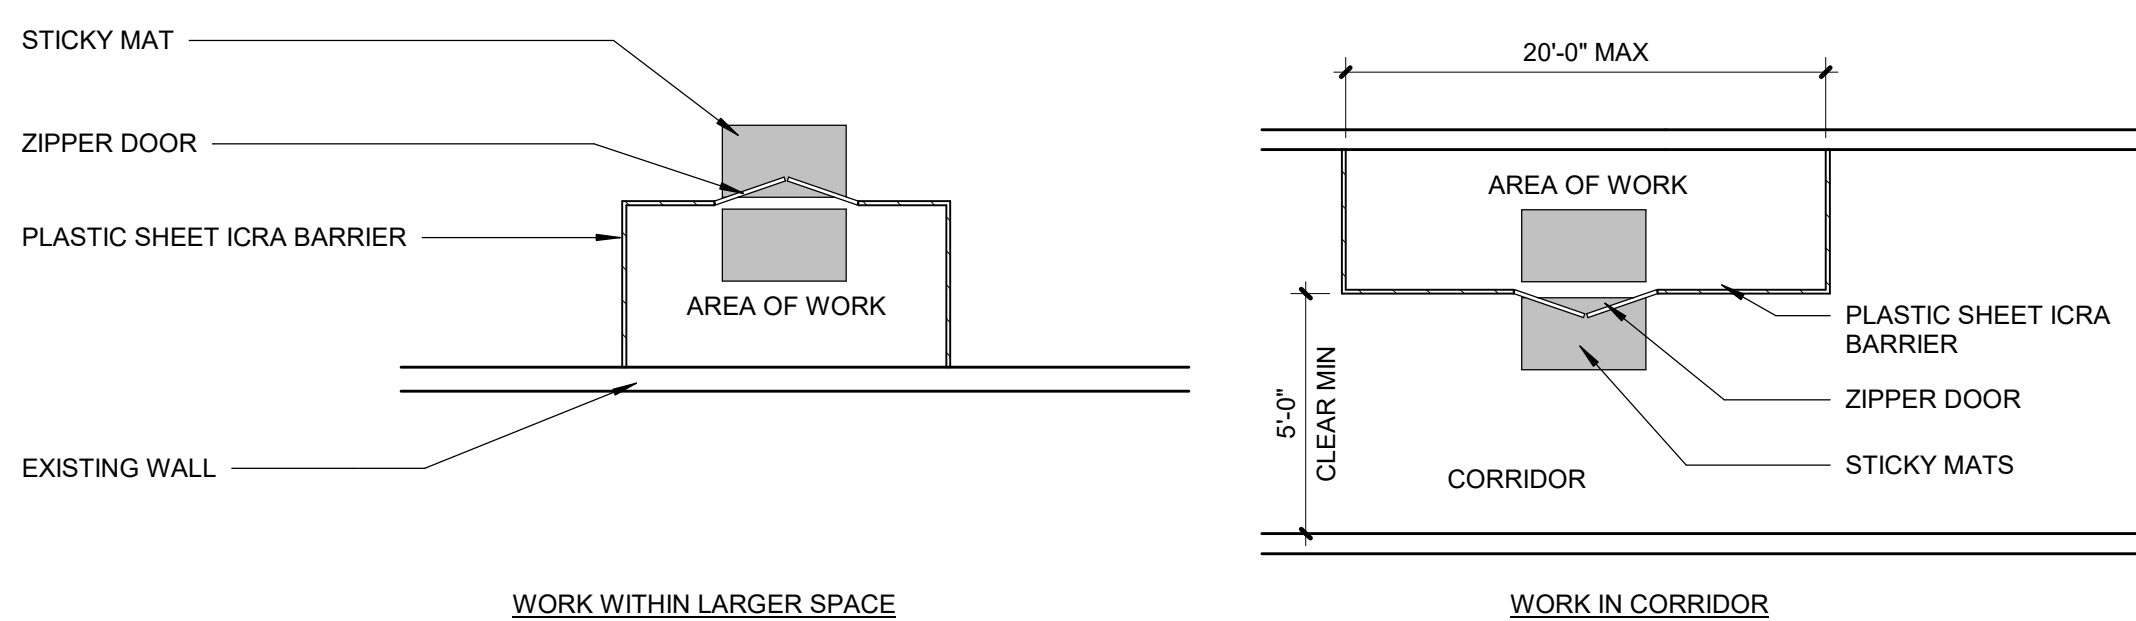

5 TYPICAL ICRA CONDITIONS
Scale: 1/4" = 1'-0"

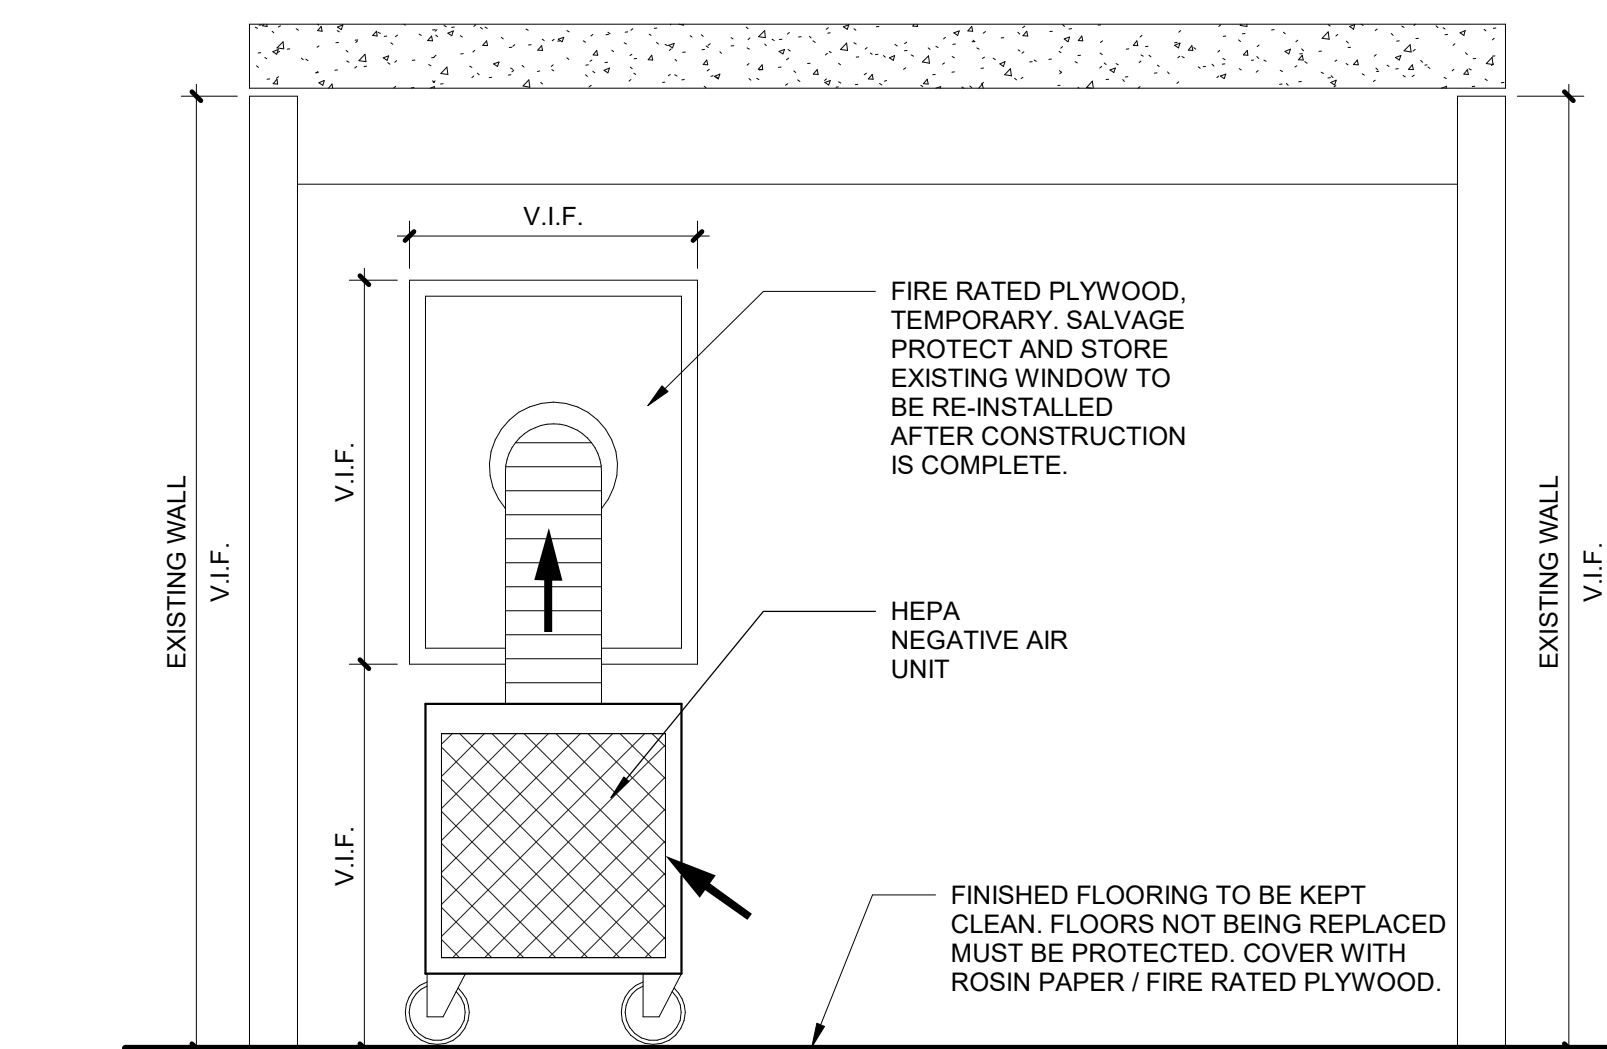

2 CROSS SECTION "A"
Scale: 1/2" = 1'-0"

ICRA NOTES

DUST CONTROL PLAN NOTES

AFter EACH PHASE, PERFORM TASKS STATED IN NOTE 5A.

1. PROVIDE STICKY MATS AND BLANKET AT THE PLASTIC BARRIER ENTRANCE SPACES (CONSTRUCTION ANTEROOM) AND CHANGE DAILY OR MORE OFTEN AS NEEDED TO PREVENT THE SPREAD OF DUST AND DEBRIS INTO ADJACENT CLEAN SPACE.

INTERNAL DEMOLITION AND CONSTRUCTION ACTIVITIES DUST AND DEBRIS CONTROL

2. USE CORRIDORS AS PRIMARY CONSTRUCTION ACCESS.

2A. TRAFFIC CONTROL: DESIGNATED ENTRY AND EXIT PROCEDURES SHALL BE DEFINED. EGRESS PATHS SHALL BE FREE OF DEBRIS; DESIGNATED ELEVATORS SHALL BE USED DURING SCHEDULED TIMES; AND ONLY AUTHORIZED PERSONNEL SHALL BE ALLOWED TO ENTER THE CONSTRUCTION ZONE. SIGNAGE SHALL DIRECT PEDESTRIAN TRAFFIC AWAY FROM THE CONSTRUCTION AREA AND MATERIALS.

3. CONTRACTOR SHALL USE TWO CARTS TO TRANSFER CONSTRUCTION MATERIAL IN AND OUT OF THE PROJECT - A CLEAN CART SHALL BE USED; THE NOT-SO-CLEAN CART SHALL BE USED BETWEEN THE MAIN ENTRY AND THE CONSTRUCTION STAGING/PREP AREA.

3A. DEMOLITION DEBRIS: DEBRIS SHALL BE REMOVED IN CARTS WITH TIGHTLY FITTED COVERS, USING DESIGNATED TRAFFIC ROUTES. EFFORTS SHALL BE MADE TO MINIMIZE USE OF ELEVATORS WITH AN EMPHASIS ON TRANSPORT DURING THE LOWEST PERIOD OF ACTIVITY. DEBRIS SHALL BE REMOVED DAILY AND AT TIMES SPECIFIED BY THE VAMC. IF CHUTES ARE USED TO DIRECT DEBRIS OUTSIDE, HIGH EFFICIENCY PARTICULATE AIR (HEPA) FILTERED NEGATIVE AIR MACHINES SHALL BE USED; AND THE CHUTE OPENING SHALL BE SEALED WHEN NOT IN USE. FILTERS SHALL BE BACKED UP SYSTEMS OF ADJACENT AREAS. USE OF THE NEGATIVE AIR PRESSURE SYSTEM WITHIN THE ENCLOSURE TO REMOVE DUST SHALL PASS AIR THROUGH AN INDUSTRIAL GRADE, PORTABLE HEPA FILTER CAPABLE OF FILTRATION RATES OF 300-800 CUBIC FEET PER MINUTE (FT3/MIN), OR EXHAUST AIR DIRECTLY TO THE OUTSIDE IF APPROVED BY VAMC. IF EXHAUST SHALL BE TIED INTO A RE-CIRCULATED AIR SYSTEM, A PRE-FILTER AND HEPA FILTER SHALL BE USED BEFORE EXHAUST TO PREVENT CONTAMINATION OF THE DUCTS.

3B. EXTERIOR WINDOWS: WINDOWS SHALL BE SEALED TO MINIMIZE INFILTRATION FROM ANY ADJACENT EXCAVATION DEBRIS.

3C. ALL EQUIPMENT REMAIN IN THE ORs AND ASSOCIATED ROOMS SHALL BE COVERED AND PROTECTED PRIOR STARTING EACH CONSTRUCTION PHASE.

VENTILATION AND ENVIRONMENTAL CONTROLS

4. AIR SYSTEM FLOW: THE CORVA VERIFY AND ACKNOWLEDGE CONTRACTOR WHETHER THE CONSTRUCTION AREA USES FRESH/OUTSIDE OR RE-CIRCULATED AIR; FILTERS SHALL BE ADDED OR RETURN VENTS COVERED AS NEEDED WITH FILTER MATERIAL OR PLASTIC. AIR MUST FLOW FROM CLEAN TO DIRTY AREAS.

4A. NEGATIVE AIR PRESSURE: THE AIR WITHIN THE CONSTRUCTION AREA SHALL BE NEGATIVE WITH RESPECT TO SURROUNDING AREAS AND WITH NO DISRUPTION OF AIR SYSTEMS OF ADJACENT AREAS. USE OF THE NEGATIVE AIR PRESSURE SYSTEM WITHIN THE ENCLOSURE TO REMOVE DUST SHALL PASS AIR THROUGH AN INDUSTRIAL GRADE, PORTABLE HEPA FILTER CAPABLE OF FILTRATION RATES OF 300-800 CUBIC FEET PER MINUTE (FT3/MIN), OR EXHAUST AIR DIRECTLY TO THE OUTSIDE IF APPROVED BY VAMC. IF EXHAUST SHALL BE TIED INTO A RE-CIRCULATED AIR SYSTEM, A PRE-FILTER AND HEPA FILTER SHALL BE USED BEFORE EXHAUST TO PREVENT CONTAMINATION OF THE DUCTS.

4B. ADJACENT AREAS: THE STATUS OF SEALED PENETRATIONS AND INTACT CEILING SHALL BE VERIFIED DAILY.

4C. AIR EXCHANGE RATES AND PRESSURE RELATIONSHIPS: VAMC AND CONTRACTOR SHALL VERIFY AND MAINTAIN PROPER RATES IN CRITICAL AREAS NEAR CONSTRUCTION ACTIVITY AND ENSURE AIR IS NOT BEING RE-CIRCULATED WITHOUT FILTRATION FROM THE CONSTRUCTION AREA ELSEWHERE. PROVIDE AIR PRESSURE TESTING THROUGHOUT THE PROJECT IN THE FREQUENCY AS IDENTIFIED BY THE CORVA.

CONTAMINATION OF PATIENT ROOMS, SUPPLIES, EQUIPMENT AND RELATED AREAS

5. WORKSITE CLOTHING: CONTRACTOR PERSONNEL CLOTHING SHALL BE FREE OF LOOSE SOIL AND DEBRIS BEFORE LEAVING THE CONSTRUCTION AREA. IF PROTECTIVE APPAREL IS NOT WORN (E.G., COVERALLS, FOOTGEAR AND HEADGEAR) A HEPA-FILTERED VACUUM SHALL BE USED TO REMOVE DUST FROM CLOTHING BEFORE LEAVING THE BARRICADE. IF PROTECTIVE APPAREL IS UTILIZED, THE CONTRACTOR SHALL CONSTRUCT A SPACE OR ANTEROOM FOR CHANGING CLOTHING AND STORING EQUIPMENT (DESIGNATED AREA, ALL EQUIPMENT, TOOLS, TOOL CARTS, AND MATERIALS TRANSPORTED THROUGH OCCUPIED AREAS SHALL BE MADE FREE FROM DUST AND MOISTURE BY VACUUMING AND WET WIPING BEFORE THEIR REMOVAL FROM THE CONSTRUCTION ZONE OR WORK AREA.

5A. POST CONSTRUCTION: DO NOT REMOVE BARRIERS AND KEEP ALL HVAC ISOLATION UNTIL CONTRACTOR HAS CLEANED CONSTRUCTION SITE, VA EMS STAFF HAS DONE A TERMINAL CLEANING, AND VA INFECTIOUS DISEASE CONTROL HAS INSPECTED AND APPROVED THE CLEANING.

INFECTION CONTROL RISK MITIGATION RECOMMENDATIONS MATRIX OF PRECAUTIONS FOR CONSTRUCTION AND RENOVATION

Type of Construction / Project Activity Table	
TYPE A	Inspection and Non-Invasive Activities Includes, but is not limited to: - removal of ceiling tiles for visual inspection limited to 1 tile to 50 square feet - painting (but not sanding), wall covering - electrical trim work, minor plumbing, and activities which do not generate dust or require cutting of walls or access to ceilings other than for visual inspection
TYPE B	Small scale, short duration activities which create minimal dust Includes, but is not limited to: - installation of telephone and computer cabling - access to chase spaces - cutting of walls or ceiling where dust migration can be controlled
TYPE C	Work that generates a moderate to high level of dust or requires demolition or removal of any fixed building components or assemblies Includes, but is not limited to: - sanding of walls for painting or wall covering - removal of floor coverings, ceiling tiles and casework - new wall construction - minor dust work or electrical work above ceilings - major cabling activities - any activity which cannot be completed within a single work shift
TYPE D	Major demolition and construction projects Includes, but is not limited to: - activities which require consecutive work shifts - requires heavy demolition or removal of a complete ceiling system - new construction

Patient Risk Group Table			
Group 1 Low Risk	Group 2 Medium Risk	Group 3 High Risk	Group 4 Highest Risk
- Office areas (non-clinical) - Hallways - FES/EMS areas	- Bldg #69 Therapy areas - Respiratory Therapy - Outpatient Clinics - OB/GYN - Mental Health Units - VACANT AREA ADJACENT TO OCCUPIED AREA	- Pharmacy - Radiology/CT Scanner - Urgent Care - Laboratories	- CLCs - SPD, AMCU, - Respiratory Isolation Rooms - Surgery

Patient Risk Group	Construction Project Type			
	TYPE A	TYPE B	TYPE C	TYPE D
LOW Risk Group 1	I	I	II	III/IV
MEDIUM Risk Group 2	I	I	III	IV
HIGH Risk Group 3	II	III	III/IV	IV
HIGHEST Risk Group 4	III	III/IV	III/IV	IV

Note: Infection Control approval will be required when the Construction Activity and Risk Level indicate that Class II or Class III control procedures are necessary.

It is the Contractor's Responsibility to provide the following Infection Control Precautions depending upon the Area Class Designation

	During Construction Project	Upon Completion of Project
CLASS I	1. Execute work by methods to minimize raising dust from construction operations. 2. Immediately replace a ceiling tile displaced for visual inspection.	1. Wipe surfaces to remove dust.
CLASS II	1. Includes all activities required by Class I 2. Provide active means to prevent airborne dust from dispersing into atmosphere. 3. Water mist work surfaces to control dust while cutting. 4. Seal unused doors with dust tape. 5. Block off and seal air vents. 6. Replace adhesive walk-off mats at entrance and exit of work area. Replace used mats in accordance with manufacturer's recommendations. 7. Remove or isolate HVAC system in area where work is being done to prevent contamination of duct system.	1. Wipe work surfaces with disinfectant. 2. Contain construction waste before transport in tightly covered containers. 3. Wet mop and/or vacuum work area with HEPA filtered vacuum before leaving work areas. 4. Remove isolation of HVAC system in areas where work is being performed.
CLASS III	1. Includes all activities required by Class II 2. Obtain Infection Control Permit from Hospital Safety Officer or Facilities Management Maintenance and Engineering department before construction begins. 3. Remove or isolate HVAC system in area where work is being done to prevent contamination of duct system. 4. Complete all critical barriers before construction begins or implement control cube method. 5. Maintain negative air pressure within work site utilizing HEPA-equipped air filtration units. 6. Contain construction waste before transport in tightly covered containers. 7. Cover transport receptacles or carts. Tape covers. 8. Wet mop and/or vacuum with HEPA filtered vacuum before leaving work areas. 9. Remove isolation of HVAC system in areas where work is being performed.	1. Remove barrier materials carefully to minimize spreading of dirt and debris associated with construction. 2. Contain construction waste before transport in tightly covered containers. 3. Cover transport receptacles or carts. Tape covering. 4. Vacuum work area with HEPA-filtered vacuums. 5. Wet mop with disinfectant. 6. Remove isolation of HVAC system in areas where work is being performed.
CLASS IV	1. Includes all activities required by Class III 2. Obtain Infection Control Permit from Hospital Safety Officer or Facilities Management Maintenance and Engineering department before construction begins. 3. Isolate HVAC system in areas where work is being done to prevent contamination of duct system. 4. Complete all critical barriers before construction begins or implement control cube method before construction begins. 5. Maintain negative air pressure within work site utilizing HEPA equipped air filtration units. 6. Seal holes, pipes, conduits, and punctures appropriately. 7. Construct anteroom and require all personnel to pass through this room so they can be vacuumed using a HEPA vacuum cleaner before leaving work site or they can wear cloth or paper coveralls that are removed each time they leave the work site. 8. All personnel entering work site are required to wear shoe covers. Shoe covers must be changed each time the worker exits the work area. 9. Place adhesive walk-off mats at entrance to work area within anteroom. 10. Replace per manufacturer's recommendations. Do not remove barriers from work area until completed project is inspected each by the Hospital Safety Officer, Facilities Management Maintenance and Engineering Department and thoroughly cleaned by the Hospital Environmental Services Department or their contracted Environmental Service Company. 11. Cover transport receptacles or carts. Tape covering. 12. Vacuum work area with HEPA filtered vacuums. 13. Wet mop with disinfectant after barriers are removed. 14. Remove isolation of HVAC system in areas where work is being performed.	1. Remove barrier materials carefully to minimize spreading of dirt and debris associated with construction. 2. Contain construction waste before transport in tightly covered containers. 3. Cover transport receptacles or carts. Tape covering. 4. Vacuum work area with HEPA filtered vacuums. 5. Wet mop area with disinfectant after barriers are removed. 6. Remove or isolate HVAC system in areas where work was being performed.

THIS MATRIX NEEDS TO BE VERIFIED WITH THE CORVA, PRIOR TO IMPLEMENTATION, AS THE CORVA MAY HAVE THEIR OWN ICRA MATRIX.

FULLY SPRINKLERED
100% CONSTRUCTION DOCUMENTS

CONSULTANTS:			PROJECT MANAGER		ACG Project Number 22-038		Office of Construction and Facilities Management		Drawing Title ICRA INFORMATION AND DETAILS		Project Title REMOVE AND REPLACE PUBLIC ADDRESS SYSTEM		VA PROJECT NUMBER 548-22-100	
			Headquarters: Apogee Consulting Group, P.A. 1151 Kildaire Farm Road, Suite 120 Cary, North Carolina 27511						Location WEST PALM BEACH VAMC 7305 NORTH MILITARY TRAIL WEST PALM BEACH FL, 33410-6400		Approved		Building Number AS NOTED	
			Engineers Architects www.acg-pa.com 919-858-7420				U.S. Department of Veterans Affairs				Date DECEMBER 14, 2022		Checked DJR	
											Drawn LMB		Drawing Number G-003	
													Dwg 3 of 4	

ELECTRICAL GENERAL NOTES

1. ALL ELECTRICAL DEVICES, FIXTURES, EQUIPMENT AND FEEDERS SHALL BE INSTALLED IN ACCORDANCE WITH THE PROJECT SPECIFICATIONS, THE MANUFACTURER'S RECOMMENDED PROCEDURES, ALL APPLICABLE LOCAL AND STATE CODES, AMERICANS WITH DISABILITIES ACT AND WITH THE LATEST EDITION OF THE NATIONAL ELECTRICAL CODE AND VA STANDARDS.
2. PROVIDE ADDITIONAL SUPPORT FOR DEVICES, FIXTURES, EQUIPMENT AND FEEDERS WHERE THE BUILDING CONSTRUCTION IS NOT SUITABLE FOR DIRECT MOUNTING.
3. FIRESTOP, DRAFTSTOP, SMOKESTOP AND/OR PROTECT THE ANNULAR SPACE AROUND ALL PENETRATIONS THROUGH WALLS, PARTITIONS, FLOORS, CEILING, AND ROOFS IN ACCORDANCE WITH THE REQUIREMENTS OF THE NATIONAL ELECTRICAL CODE, UL LISTING REQUIREMENT AND THE APPLICABLE BUILDING CODES.
4. VERIFY CEILING SYSTEMS AND PROVIDE MOUNTING ACCESSORIES, TRIMS AND ALL REQUIRED MOUNTING HARDWARE TO SUIT THE PARTICULAR INSTALLATION.
5. PROTECT EXISTING UNDERGROUND AND BUILDING INTERIOR UTILITIES DURING CONSTRUCTION.
6. BRANCH CIRCUIT CONDUCTORS SHALL BE 12 AWG COPPER MINIMUM.
7. COORDINATE ANY AND ALL WORK WITH ALL OTHER TRADES PRIOR TO INSTALLATION SO AS TO AVOID CONFLICT DURING CONSTRUCTION.
8. ALL PANELS SHALL HAVE TYPED, COMPLETED DIRECTORIES INDICATING EQUIPMENT SERVED AND ROOM NUMBER (AS INDICATED ON FINAL BUILDING ROOM SIGNAGE) OF EQUIPMENT LOCATION, OR SPARE, OR SPACE.
9. MANUFACTURER'S NAME AND MODEL NUMBER ARE GIVEN FOR DESCRIPTIVE PURPOSES, TO INDICATE A QUALITY STANDARD, AND ARE NOT INTENDED TO LIMIT PRODUCTS TO A PARTICULAR MANUFACTURER. PRODUCTS DEEMED EQUAL AND APPROVED BY THE DESIGNER WILL BE ACCEPTED. ALL PRODUCTS MUST COMPLY WITH "BUY AMERICAN ACT".
10. ALL FEEDERS AND CIRCUITRY SHALL BE TORQUED PER THE PANEL, BREAKER, AND/OR PARTICULAR EQUIPMENT MANUFACTURER'S SPECIFICATIONS.
11. CIRCUITRY TO SWITCHES, RECEPTACLES, AND ALL OTHER DEVICES SHALL BE TERMINATED ON THE DEVICE'S SCREW TERMINALS.
12. MOUNTING HEIGHTS INDICATED ARE TO CENTER OF DEVICE, OUTLET, FIXTURE, OR EQUIPMENT UNLESS NOTED OTHERWISE.
13. ALL WIRE TERMINATIONS SHALL BE RATED FOR 75 DEGREES C.
14. ALL CONDUCTORS SHALL HAVE THHN/THWN INSULATION, UNLESS OTHERWISE NOTED.
15. ALL CONDUIT SHALL BE RGS OR EMT UNLESS OTHERWISE NOTED. FMC CONDUIT SHALL BE USED ON VIBRATING EQUIPMENT (MAXIMUM LENGTH OF 6 FEET). PVC SHALL BE USED FOR UNDERGROUND CONDUIT OR WHERE CONCRETE-ENCASED. WHERE VIBRATING EQUIPMENT IS LOCATED OUTSIDE, LFMC CONDUIT SHALL BE USED (MAXIMUM SIX FEET) FOR FINAL CONNECTIONS.
16. ALL ELECTRICAL MATERIALS, DEVICES, APPLIANCES AND EQUIPMENT SHALL BE LABEL LISTED BY AN APPROVED THIRD PARTY TESTING AGENCY.
17. IN CASE OF CONFLICTS OR DISCREPANCIES WITHIN OR AMONG THE CONTRACT DRAWINGS, THE BETTER QUALITY, MORE STRINGENT REQUIREMENTS OR GREATER QUANTITY OF WORK, AS DETERMINED BY THE GOVERNMENT, SHALL BE PROVIDED.
18. COMPRESSION COUPLINGS SHALL BE USED. NO SET SCREW FITTINGS ARE ALLOWED.
19. MINIMUM CONDUIT SIZE TO BE USED IS 3/4".
20. FEEDER TAGS APPENDED WITH 'VD' ARE UPSIZED IN AMPACITY DUE TO VOLTAGE DROP.

TECHNOLOGY SYMBOL LEGEND

SYMBOL	HEIGHT	DESCRIPTION
▼N	18"	DATA OUTLET - N-4 PR UTP (N - QUANTITY)
▼N	48"	TELCO OUTLET - N-4 PR UTP (N - QUANTITY)
[NCE]	6" TO TOP	NURSE CALL EQUIPMENT CABINET
[F]	FLOOR	FOUR POST OIT EQUIPMENT RACK
[F]	FLOOR	TWO POST OIT EQUIPMENT RACK
[]	FLOOR	OIT EQUIPMENT CABINET
[]	ABOVE CEILING	LADDER CABLE TARY
—	18"	GROUND BUS
—	8"	4x8x3/4" FIRE RATED TT8
[]	FLOOR	FLOOR BOX FOR DATA
[]	CEILING	CEILING MOUNTED SPEAKER
[]	96"	WALL MOUNTED SPEAKER
[]	AS NOTED	WALL MOUNTED HORN
[]	48"	VOLUME CONTROL
[]	48"	PAGING CONSOLE
[PA]	FLOOR	PAGING CABINET
[]	AS NOTED	JUNCTION BOX, WALL MOUNTED, PURPOSE AS NOTED

DEVICES WITH THE FOLLOWING TAGS ARE AS INDICATED:
E: EXISTING DEVICES TO REMAIN. PROVIDE NEW CABLING AND CONDUIT AS NEEDED.
D: EXISTING DEVICES TO BE DEMOLISHED BY THE CONTRACTOR.
R: EXISTING DEVICES TO BE REPLACED WITH NEW BY THE CONTRACTOR.
N: NEW DEVICES TO BE PROVIDED AND INSTALLED BY THE CONTRACTOR.
ALL HEIGHTS ARE TO CENTER OF DEVICE UNLESS NOTED OTHERWISE.
ANY HEIGHTS INDICATED IN PLANS SHALL SUPERSEDE THOSE LISTED HERE.
SEE DRAWINGS FOR MORE INFORMATION.
NOTE: NOT ALL SYMBOLS ARE USED.

ELECTRICAL SYMBOL LEGEND

SYMBOL	HEIGHT	DESCRIPTION
[]	18"	120V SIMPLEX RECEPTACLE
[]	18"	120V DUPLEX RECEPTACLE
[]	18"	120V DUPLEX RECEPTACLE EMERGENCY OUTLET AND COVER PLATE SHALL BE RED IN COLOR
[]	18"	120V QUADRUPLX RECEPTACLE
[]	18"	120V QUADRUPLX RECEPTACLE EMERGENCY OUTLET AND COVER PLATE SHALL BE RED IN COLOR
[]	18"	208V DUPLEX RECEPTACLE
[]	18"	SPECIAL RECEPTACLE
[]		120V DUPLEX RECEPTACLE FLOOR BOX
[]		120V DUPLEX RECEPTACLE EMERGENCY FLOOR BOX OUTLET AND COVER PLATE SHALL BE RED IN COLOR
[]		120V QUADRUPLX RECEPTACLE FLOOR BOX
[]		120V QUADRUPLX RECEPTACLE EMERGENCY FLOOR BOX OUTLET AND COVER PLATE SHALL BE RED IN COLOR
		RECEPTACLE MODIFIERS: AC: 3" ABOVE COUNTERTOP/BACKSPLASH GFI: GROUND FAULT CURRENT INTERRUPTER WP: WEATHERPROOF ENCLOSURE DED: DEDICATED CIRCUIT
[]	AS NOTED	JUNCTION BOX, WALL MOUNTED, PURPOSE AS NOTED
[]		JUNCTION BOX, CEILING MOUNTED, PURPOSE AS NOTED
[]		JUNCTION BOX, FLOOR MOUNTED, PURPOSE AS NOTED
[]	AS NOTED	EQUIPMENT CONNECTION
[]	72" TOP	DISCONNECT SWITCH NON-FUSED
[]	72" TOP	DISCONNECT SWITCH FUSED
[]	48"	SINGLE POLE WALL SWITCH: 48" AFF STANDARD UNO
		SWITCH MODIFIERS: M: MOTOR-RATED

ALL HEIGHTS ARE TO CENTER OF DEVICE UNLESS NOTED OTHERWISE.
TOP: HEIGHT TO TOP OF DEVICE
ANY HEIGHTS INDICATED IN PLANS SHALL SUPERSEDE THOSE LISTED HERE.

TECHNOLOGY GENERAL NOTES

1. PROVIDE COMMUNICATIONS DEVICES AND EQUIPMENT IN ACCORDANCE WITH THE CONTRACT DOCUMENTS, MANUFACTURER'S RECOMMENDED PROCEDURES, ALL APPLICABLE LOCAL AND STATE CODES, AMERICANS WITH DISABILITIES ACT, LATEST EDITION OF THE NATIONAL ELECTRICAL CODE, BICSI STANDARDS, AND VA STANDARDS.
2. PROVIDE ADDITIONAL SUPPORT FOR DEVICES AND EQUIPMENT WHERE BUILDING CONSTRUCTION IS NOT SUITABLE FOR DIRECT MOUNTING.
3. FIRESTOP, DRAFTSTOP, SMOKESTOP OR PROTECT ANNULAR SPACE AROUND PENETRATIONS THROUGH WALLS, PARTITIONS, FLOORS, CEILINGS, AND ROOF IN ACCORDANCE WITH REQUIREMENTS OF NFPA 70, UL LISTING REQUIREMENT AND APPLICABLE BUILDING CODES.
4. PROVIDE CABLING THAT COMPLIES WITH THE LATEST EDITION OF TELECOMMUNICATIONS DISTRIBUTION METHOD MANUAL AND ANSITIAIEIA PUBLICATIONS.
5. COMPLY WITH THE LATEST ANSITIAIEIA 758 AND 6078 OR 607A - GROUNDING AND BONDING REQUIREMENTS FOR TELECOMMUNICATIONS IN COMMERCIAL BUILDING.
6. COMPLY WITH THE LATEST ANSITIAIEIA 5688 - COMMERCIAL BUILDING TELECOMMUNICATIONS WIRING STANDARD.
7. COMPLY WITH THE LATEST ANSITIAIEIA 5698 - COMMERCIAL BUILDING STANDARD FOR TELECOMMUNICATIONS PATHWAYS AND SPACES.
8. COMPLY WITH THE LATEST NFPA 70 NATIONAL ELECTRICAL CODE.
9. COMPLY WITH THE LATEST NFPA 99 HEALTHCARE FACILITIES CODE.
10. COMPLY WITH THE LATEST NFPA 101 LIFE SAFETY CODE.
11. COORDINATE WORK WITH ALL OTHER TRADES PRIOR TO INSTALLATION.
12. MANUFACTURER'S NAME AND MODEL NUMBER ARE GIVEN FOR DESCRIPTIVE PURPOSES TO INDICATE A QUALITY STANDARD AND ARE NOT INTENDED TO LIMIT PRODUCTS TO A PARTICULAR MANUFACTURER. PRODUCTS DEEMED EQUAL AND APPROVED BY THE COR WILL BE ACCEPTABLE. COMPLY WITH "BUY AMERICAN ACT".
13. MOUNTING HEIGHTS INDICATED ARE TO CENTER OF DEVICE, BOXES, OUTLET, OR EQUIPMENT UNLESS NOTED OTHERWISE.
14. PROVIDE RGS OR EMT CONDUIT UNLESS OTHERWISE NOTED. ALL SPEAKER CABLING FOR THE PUBLIC ADDRESS SYSTEM SHALL BE RUN IN CONDUIT.
15. PROVIDE MATERIALS, DEVICES, APPLIANCES AND EQUIPMENT LABEL LISTED BY APPROVED THIRD PARTY TESTING AGENCY.
16. NOTIFY COR REGARDING DISCREPANCY BETWEEN PLANS AND SPECIFICATIONS FOR CLARIFICATION. THE MORE STRINGENT OF THE THEM SHALL TAKE PRECEDENCE.
17. PROVIDE TIAIEIA CAT 6 COPPER OUTLETS AND CONNECTORS.
18. ALL WORK AREA OUTLETS SHALL BE 8 PIN, CAT 6 KEYSTONE JACK WIRED PER T568A OR T568B AS DIRECTED BY THE VA COR.
19. LABEL DEVICES IN ACCORDANCE WITH LATEST ANSITIA 606A OR 606B EDITION AS WELL AS THE STANDARDS SET FORTH BY THE VA HOSPITAL OIT.
20. PROVIDE A MINIMUM OF 12" CLEARANCE ABOVE THE CABLE TRAY PER TIAIEIA 569.B PARAGRAPH 4.5.6.2.
21. ALL CABLING INSTALLED ABOVE CEILING SHALL BE PLENUM RATED.
22. MINIMUM CONDUIT SIZE TO BE USED IS 3/4".
23. DEVICES PLACED IN INTERCOMMUNICATION ROOM TO BE MOUNTED ON FIRE RETARDANT PLYWOOD.
24. BASIS OF DESIGN UTILIZED IN THIS DESIGN IS THE BIAMP VOICIA PAGING SYSTEM. ALTERNATES TO THE BASIS OF DESIGN ARE ACCEPTABLE UPON MEETING OR EXCEEDING THE FUNCTIONALITY OF THE SYSTEM AS DESIGNED.
25. CONTRACTOR SHALL TRACK AND NOTE ORDER OF SPEAKERS AND DEVICES IN SPEAKER CIRCUITS, AND PROVIDE RECORD DRAWINGS INDICATING THE ORDERING OF DEVICES.


TECHNOLOGY ABBREVIATIONS LIST

ADO	AUTOMATIC DOOR OPERATOR	OC	ON CENTER
AFF	ABOVE FINISH FLOOR	OIT	OFFICE OF INFORMATION TECHNOLOGY
BOD	BASIS OF DESIGN	PACS	PHYSICAL ACCESS CONTROL SYSTEM
CCTV	CLOSED CIRCUIT TELEVISION	PAMN	PUBLIC ADDRESS AND MASS NOTIFICATION SYSTEM
COAX	COAXIAL CABLE	PB	PUSH BUTTON
COMM	COMMUNICATION	PBB	PRIMARY BONDING BUSBAR
COR	CONTRACTING OFFICER REPRESENTATIVE	PDU	RACK POWER DISTRIBUTION UNITS
DC	DOOR CONTACT SWITCH	PDE	POWER OVER ETHERNET
DN	DOWN	PR	PAIR
DO	DOOR OPERATOR	RBB	RACK BONDING BUSBAR
DVC	DIGITAL VOICE COMMAND	RX	REQUEST TO EXIT
DVR	DIGITAL VIDEO RECORDER	SBB	SECONDARY BONDING BUSBAR
E	EXISTING DEVICES	SEP	SERVICE ENTRANCE PROTECTION
EEB	EMERGENCY EXIT BUTTON	SLC	SIGNALING LINE CIRCUIT
EL	ELECTRICAL STRIKE	SM	SINGLE MODE FIBER
ETR	EXISTING TO REMAIN	TBB	TELECOM BONDING CONDUCTOR
FA	FIRE ALARM	TEL	TELEPHONE
FACP	FIRE ALARM CONTROL PANEL	TGB	TELECOM GROUND BUS BAR
FAAP	FIRE ALARM ANNUNCIATOR PANEL	TM	TELEMONITORING
FO	FIBER OPTIC	TMBG	TELECOM MAIN GROUND BUS BAR
FAGAP	FIRE ALARM GRAPHIC ANNUNCIATOR PANEL	TP	TWISTED PAIR
IT	INTERCOMMUNICATION ROOM	TR	TELECOM ROOM
MATV	MASTER ANTENNA TELEVISION	TTB	TELEPHONE TERMINAL BOARD
MM	MULTI MODE FIBER	TV	TELEVISION
NAC	NETWORK APPLIANCE CIRCUIT PANEL	WM	WIRE MANAGEMENT
N	NEW DEVICES	WAP	WIRELESS ACCESS POINT
NCA	NETWORK CONTROL ANNUNCIATOR	UL	UNDERWRITERS LABORATORY
NS	NO SCALE	UPS	UNINTERRUPTIBLE POWER SUPPLY
NTS	NOT TO SCALE	UTP	UNSHIELDED TWISTED PAIR
NVR	NETWORK VIDEO RECORDER		

CABLES AND CONNECTORS COLOR LEGEND

DESCRIPTION ITEM	JACK	CABLE	PATCH CABLES	CONDUIT	I.D.	NOTES
DATA/COMPUTER	BLUE	BLUE	BLUE	-	C	4 PAIR CABLE
FIBER - MULTI-MODE	BLACK	AQUA	AQUA	BLUE	FO	6/12/24/36
FIBER - SINGLE-MODE	IVORY	YELLOW	YELLOW	BLUE	FO	6/12
SOUND SYSTEM	N/A	GREEN	N/A	BLUE	SS	MULTI COLOR CONDUCTORS


FULLY SPRINKLERED
100% CONSTRUCTION DOCUMENTS

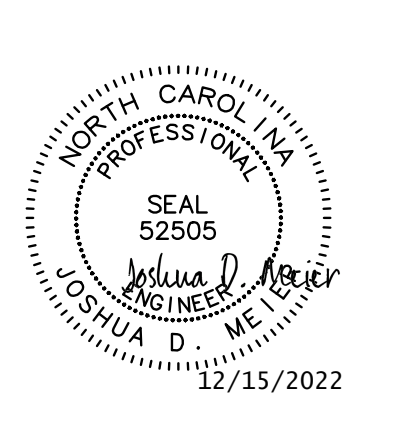			CONSULTANTS:						PROJECT MANAGER  Headquarters: Apogee Consulting Group, P.A. 1151 Kildaire Farm Road, Suite 120 Cary, North Carolina 27511 www.acg-pa.com 919-858-7420		Office of Construction and Facilities Management  U.S. Department of Veterans Affairs		Drawing Title TECHNOLOGY GENERAL NOTES, SYMBOL LEGEND, AND ABBREVIATIONS Location WEST PALM BEACH VAMC 7305 NORTH MILITARY TRAIL WEST PALM BEACH FL, 33410-6400		Project Title REMOVE AND REPLACE PUBLIC ADDRESS SYSTEM Approved Date DECEMBER 14, 2022		Checked JDM Drawn JDM		VA PROJECT NUMBER 548-22-100 Building Number # Drawing Number T-001 Dwg 1 of 32	
#	Revisions:	Date																		



AND REPLACE ADDRESS SYSTEM		VA PROJECT NUMBER 548-22-100	
		Building Number #	
		Drawing Number T-101	
Checked JDM	Drawn HT	Dwg 2 of 32	

A	VA PROJECT NUMBER 548-22-100
	Building Number #
	Drawing Number T-101
	Page 2 of 32

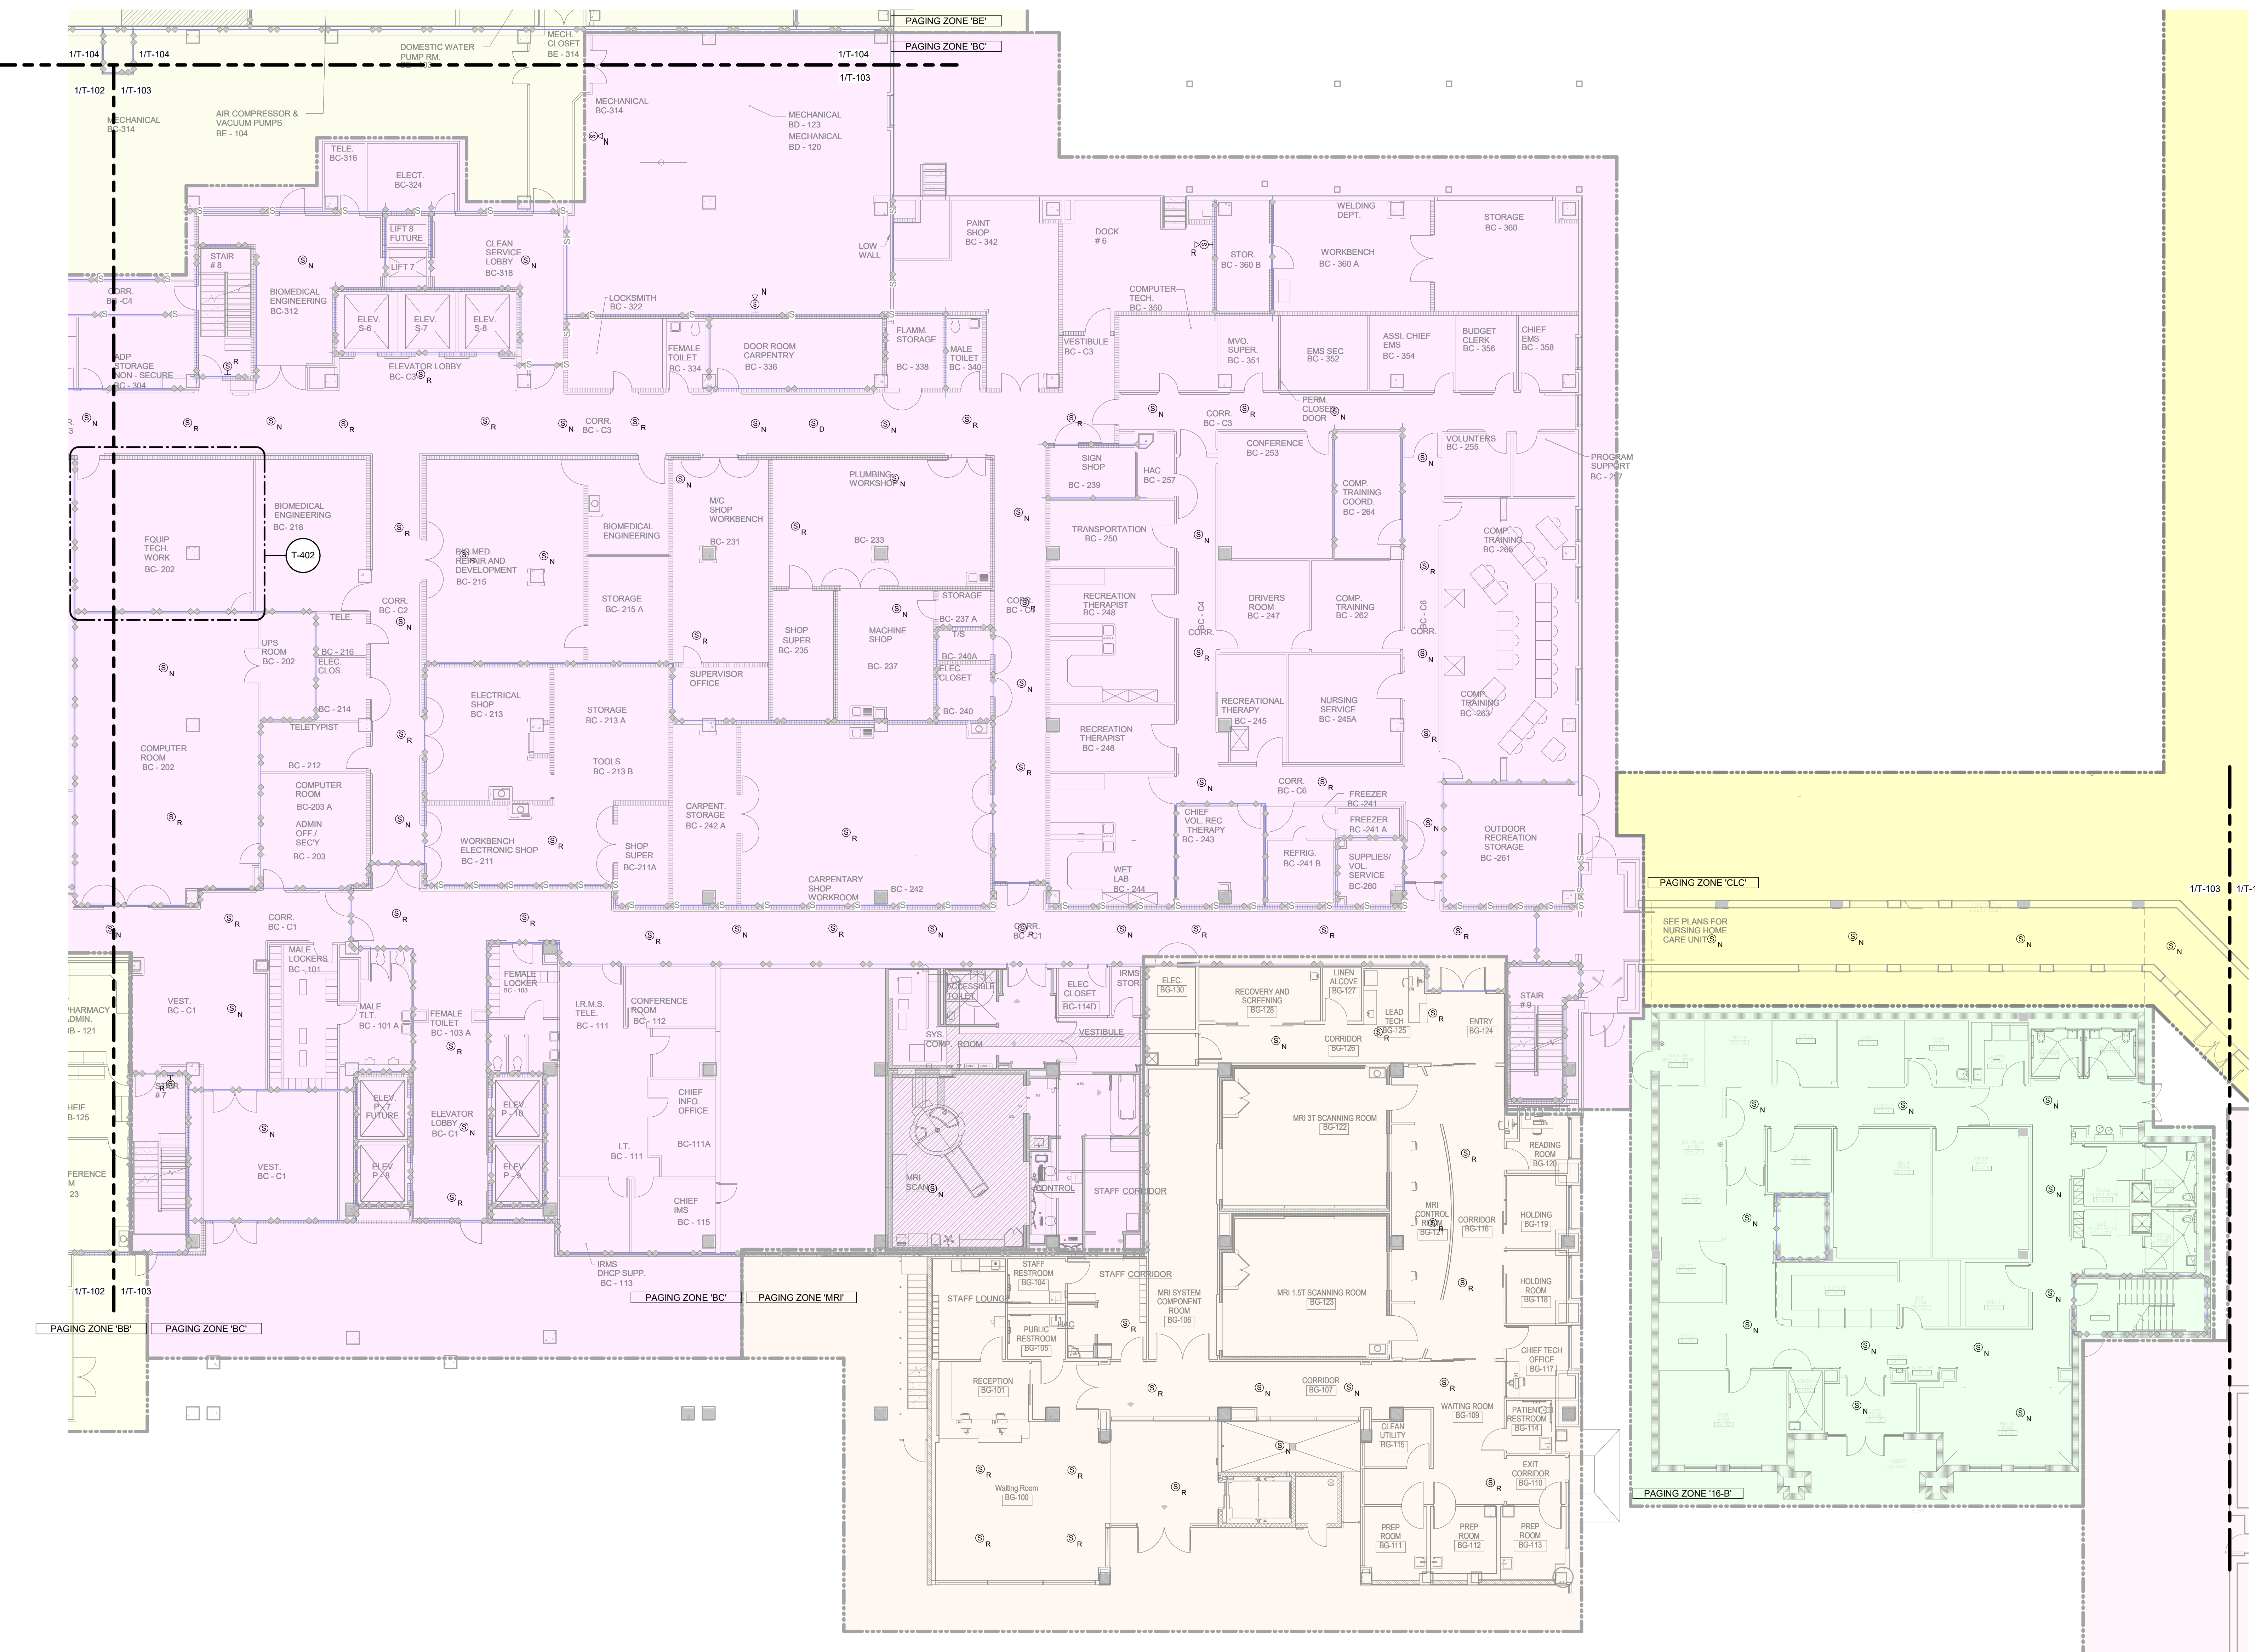

SHEET NOTES:

- A. PROVIDE PAMNS DEVICES AT LOCATIONS INDICATED ON PLANS. PROVIDE WIRING AND CIRCUIT AS INDICATED ON DETAILS.
- B. ALL PAMN WIRING SHALL BE CONCEALED IN WALLS, IN RACEWAY OR AND ABOVE THE CEILING IN CONDUIT.
- C. PAMN WIRING IN UNFINISHED AREAS SHALL BE IN SURFACE MOUNTED RACEWAY (MECH. ROOM, ROOMS WITH NO CEILINGS.)
- D. ALL CEILING SPEAKERS SHALL BE SET AT 1/2 WATT UNLESS NOTED OTHERWISE.
- E. ALL WALL MOUNTED SPEAKERS SHALL BE SET AT 4 WATTS UNLESS NOTED OTHERWISE.
- F. CONTRACTOR RESPONSIBLE FOR PROVIDING AND INSTALLING FIRE SLEEVES FOR FIREWALL. CONTRACTOR SHALL ADEQUATELY REPAIR ANY FIREWALL PENETRATIONS.

KEY NOTES:

- #

ABBREVIATED SYMBOL LEGEND

SYMBOL	HEIGHT	DESCRIPTION
Ⓢ	CEILING	CEILING MOUNTED SPEAKER
Ⓢ	96"	WALL MOUNTED SPEAKER
Ⓢ	AS NOTED	WALL MOUNTED HORN
Ⓢ	48"	VOLUME CONTROL
Ⓢ	48"	PAGING CONSOLE
Ⓢ	FLOOR	PAGING CABINET

DEVICES WITH THE FOLLOWING TAGS ARE AS INDICATED:
E. EXISTING DEVICES TO REMAIN. PROVIDE NEW CABLING AND CONDUIT AS NEEDED.
D. EXISTING DEVICES TO BE DEMOLISHED BY THE CONTRACTOR.
R. EXISTING DEVICES TO BE REPLACED WITH NEW BY THE CONTRACTOR.
N. NEW DEVICES TO BE PROVIDED AND INSTALLED BY THE CONTRACTOR.
ALL HEIGHTS ARE TO CENTER OF DEVICE UNLESS NOTED OTHERWISE. HEIGHTS INDICATED IN PLANS SHALL SUPERSEDE THOSE LISTED HERE.

KEY PLAN

SCALE: NO SCALE


SCOPE OUTLINE
AREA OF WORK

WALL RATING LEGEND


- 1 HR - FIRE SEPARATION
- 2 HR - FIRE SEPARATION
- SMOKE RESISTIVE HAZARDOUS AREA

FULLY SPRINKLERED
100% CONSTRUCTION DOCUMENTS


1 BASEMENT FLOOR NW PAMNS
Scale: 3/32" = 1'-0"

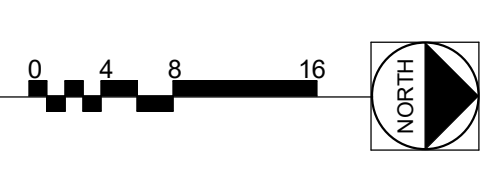

CONSULTANTS:		PROJECT MANAGER ACG Project Number 22-038 Headquarters: Apogee Consulting Group, P.A. 1151 Kildaire Farm Road, Suite 120 Cary, North Carolina 27511 www.acg-pa.com 919-858-7420		Office of Construction and Facilities Management U.S. Department of Veterans Affairs		Drawing Title BASEMENT FLOOR NW PAMNS Location WEST PALM BEACH VAMC 7305 NORTH MILITARY TRAIL WEST PALM BEACH FL, 33410-6400		Project Title REMOVE AND REPLACE PUBLIC ADDRESS SYSTEM Approved Date DECEMBER 14, 2022 Checked JDM Drawn HT		VA PROJECT NUMBER 548-22-100 Building Number # Drawing Number T-103 Dwg 4 of 32	
# Revisions:											
Date											

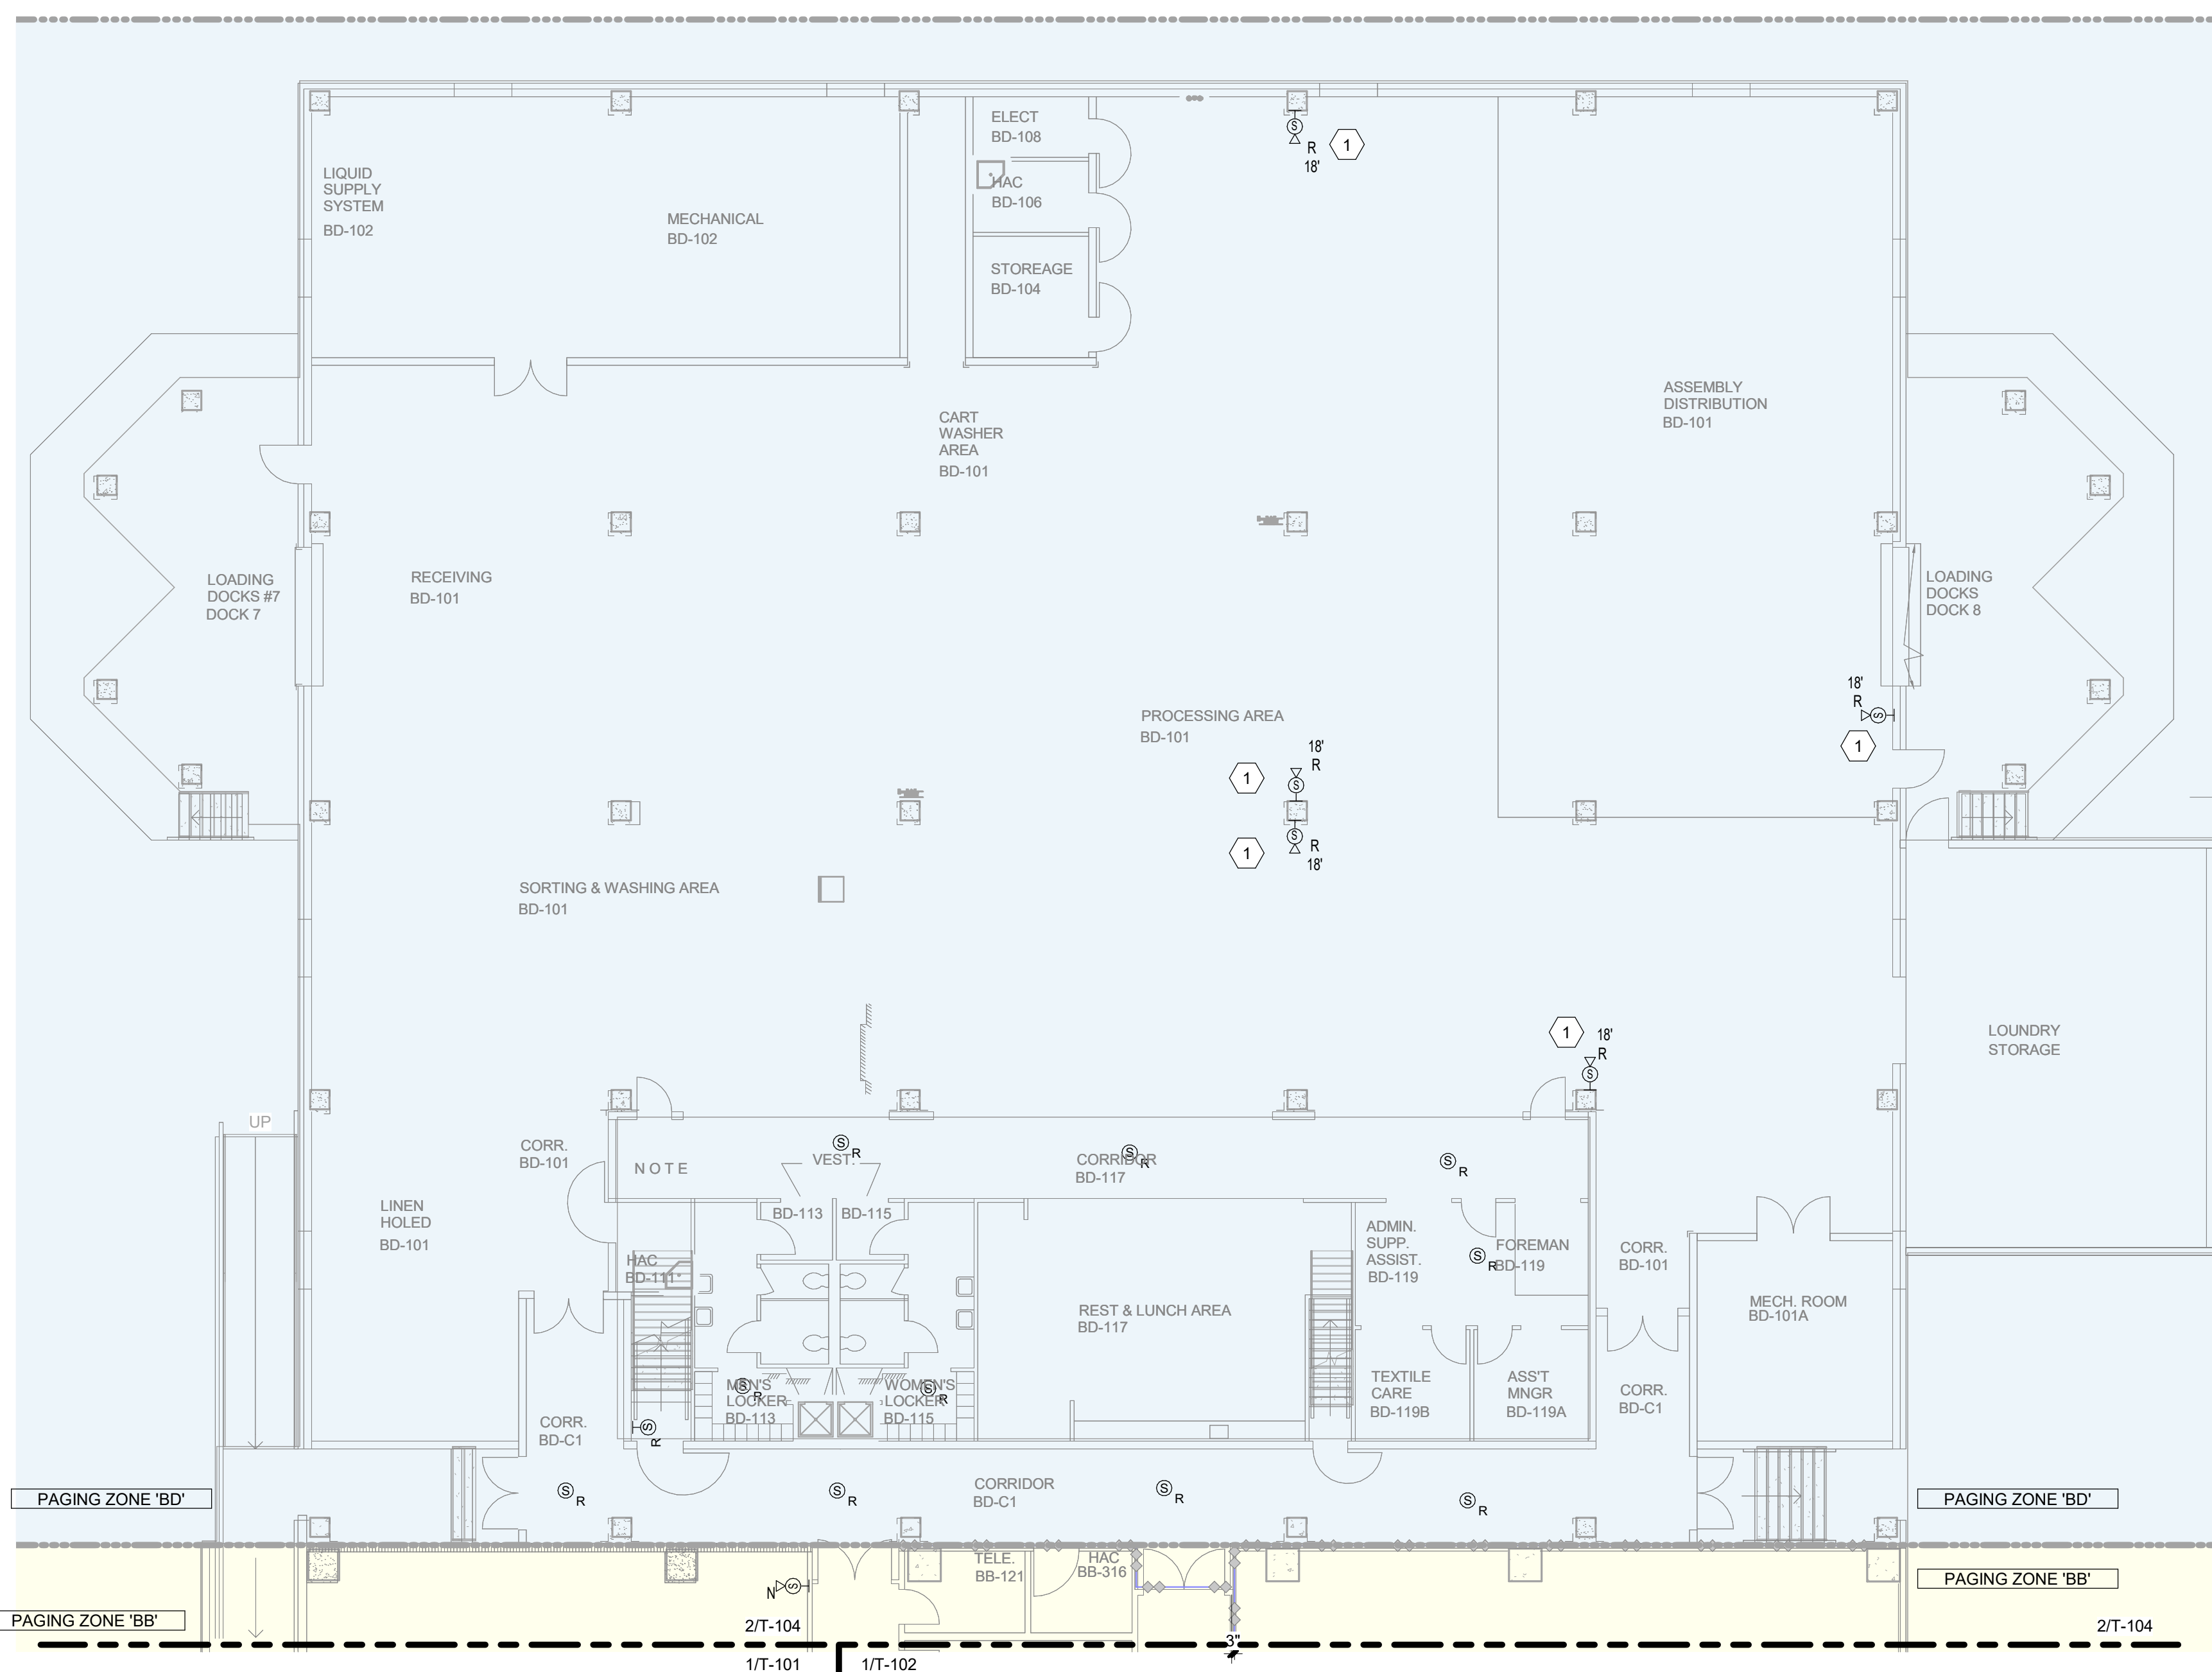

2 BASEMENT FLOOR PAMNS - LAUNDRY ROOM
Scale: 3/32" = 1'-0"

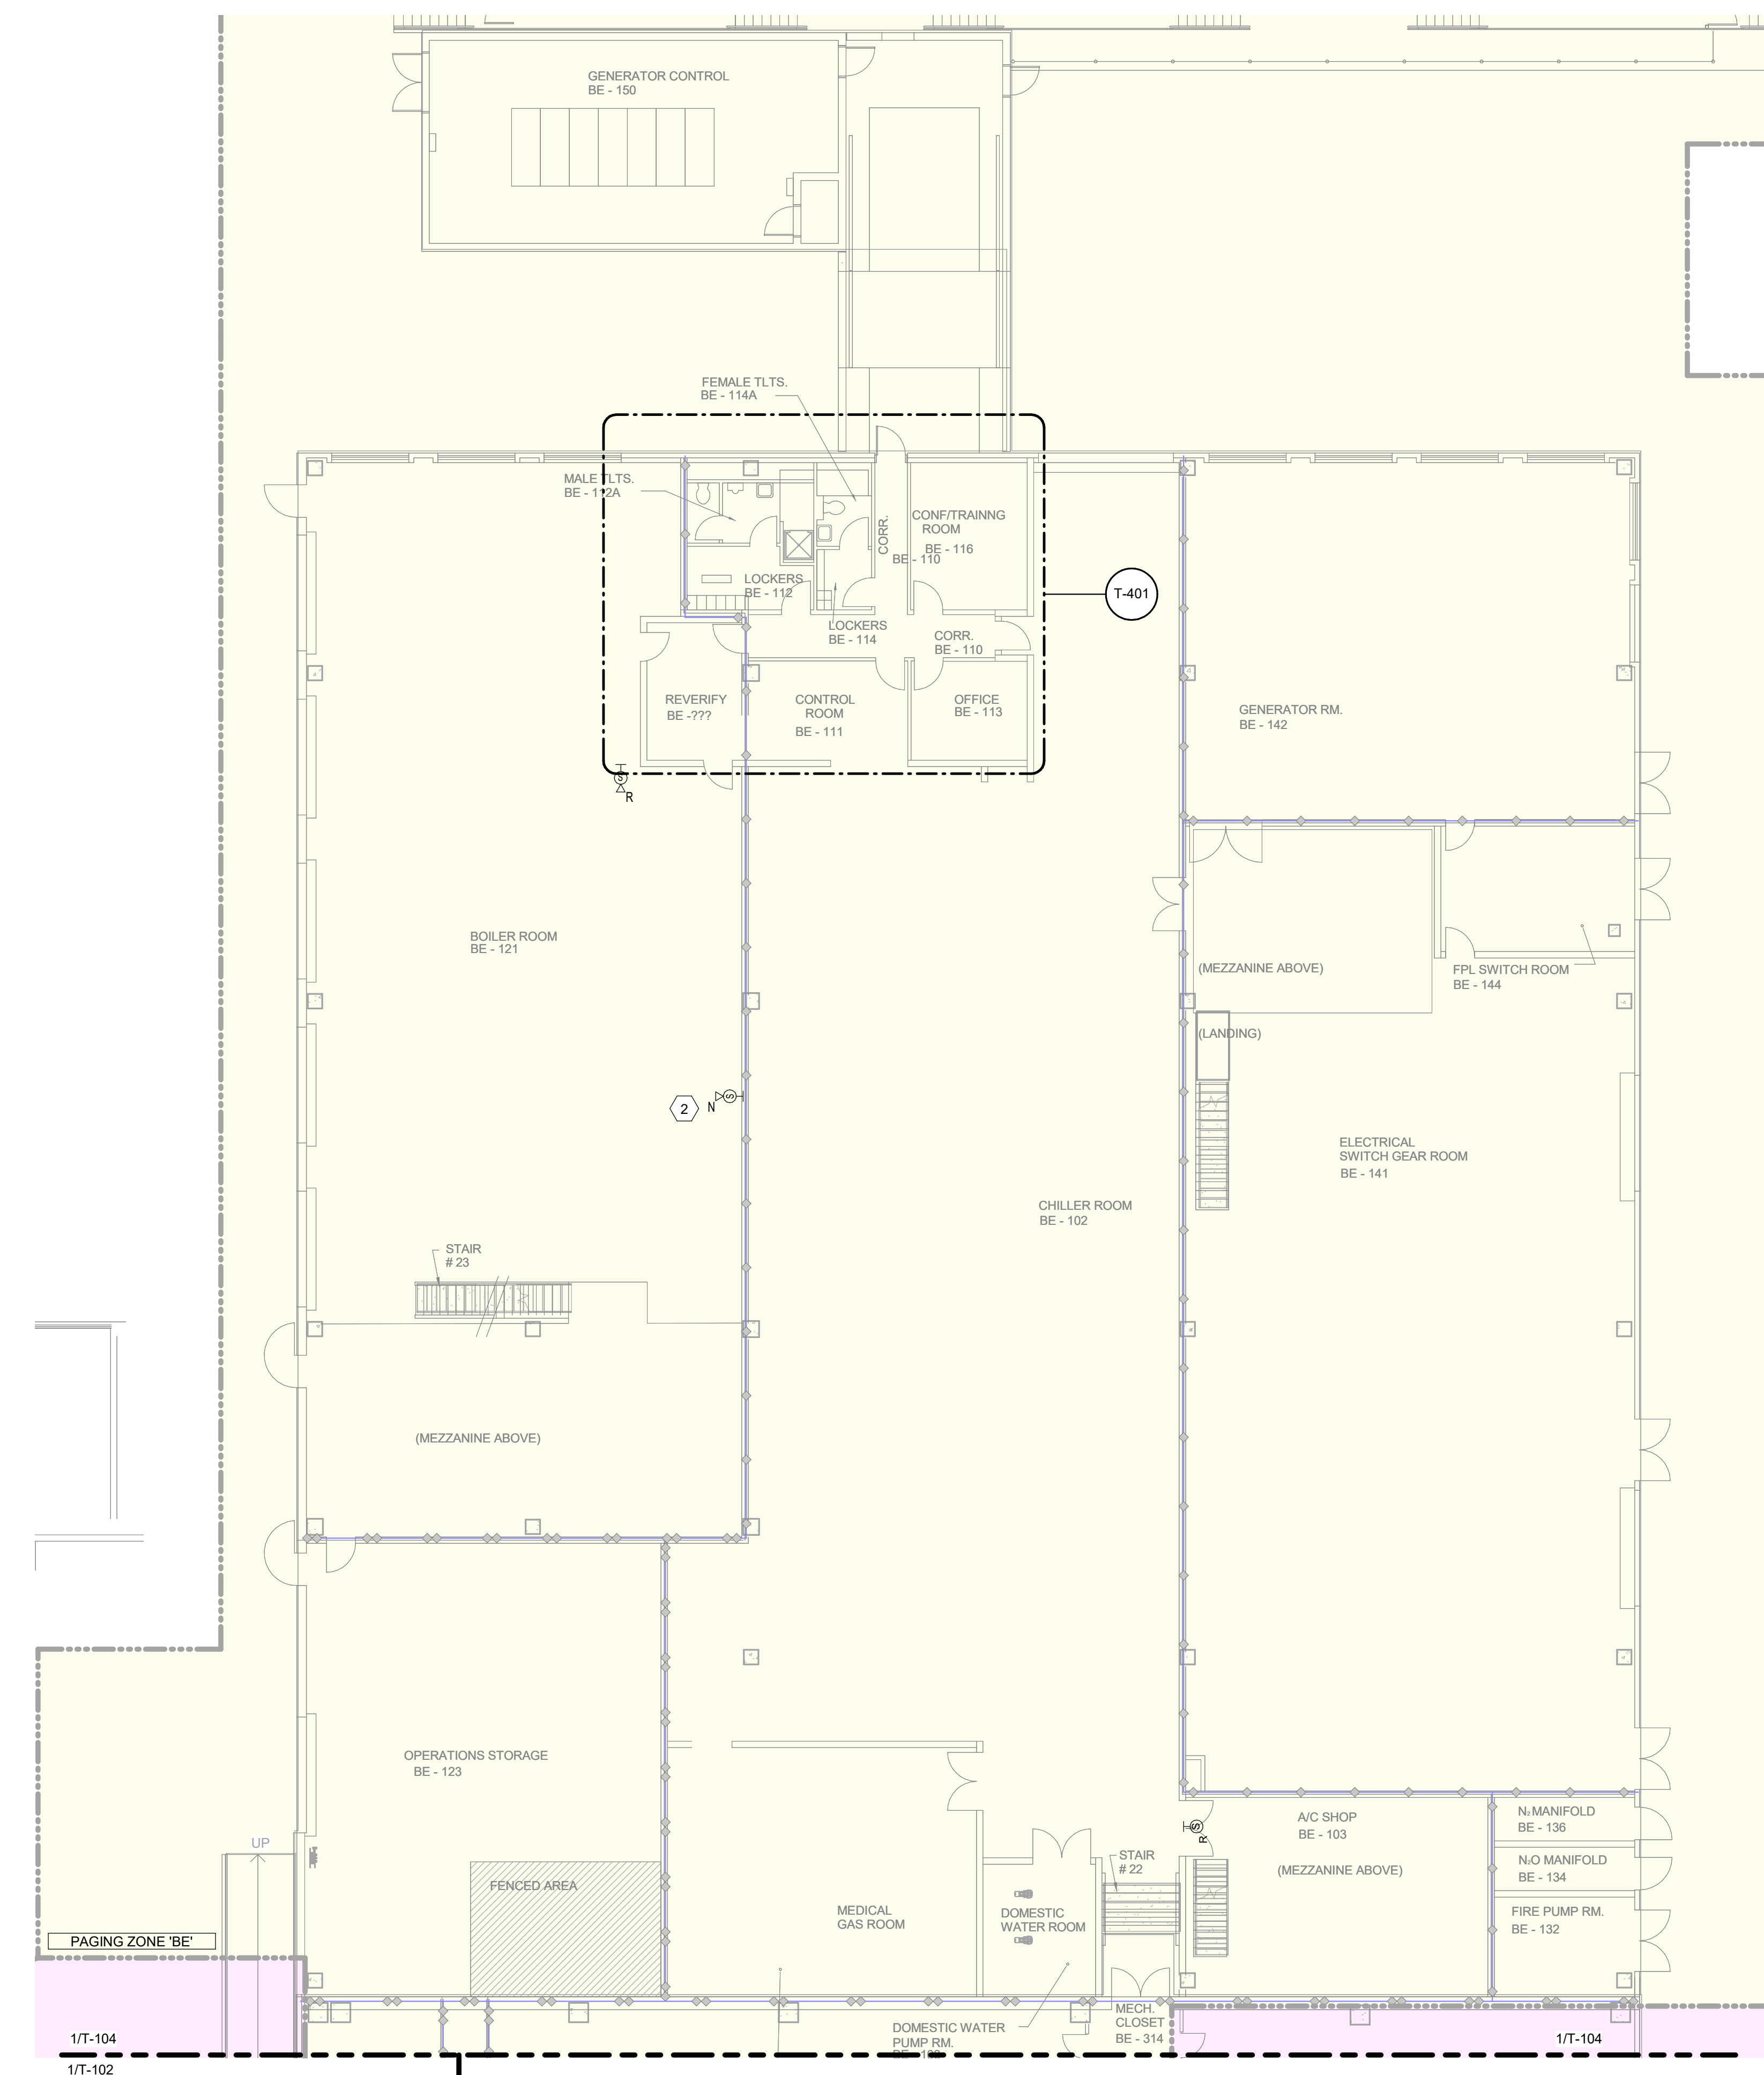

1 BASEMENT FLOOR PAMNS - ENERGY CENTER
Scale: 3/32" = 1'-0"

- ## SHEET NOTES:
- A. PROVIDE PAMMS DEVICES AT LOCATIONS INDICATED ON PLANS. PROVIDE WIRING AND CIRCUIT AS INDICATED ON DETAILS.
 - B. ALL PAMM WIRING SHALL BE CONCEALED IN WALLS, IN RACEWAY OR AND ABOVE THE CEILING CONDUIT.
 - C. PAMM WIRING IN UNFINISHED AREAS SHALL BE IN SURFACE MOUNTED RACEWAY (MECH. ROOM, ROOMS WITH NO CEILINGS.)
 - D. ALL CEILING SPEAKERS SHALL BE SET AT 1/2 WALL UNLESS NOTED OTHERWISE.
 - E. ALL WALL MOUNTED SPEAKERS SHALL BE SET AT 4 WALLS UNLESS NOTED OTHERWISE.
 - F. CONTRACTOR RESPONSIBLE FOR PROVIDING AND INSTALLING FIRE SLEEVES FOR FIREWALL. CONTRACTOR SHALL IMMEDIATELY REPAIR ANY FIREWALL PENETRATIONS.

KEY NOTES:

- 1 COORDINATE PLACEMENT OF DEVICES IN LAUNDRY PROCESSING AREA WITH EXISTING EQUIPMENT IN SPACE. HORNS IN THIS AREA SHALL BE MOUNTED ABOVE RAIL SYSTEM IN AREA.
- 2 COORDINATE PLACEMENT OF HORN WITH EXISTING DEVICES ON WALL.

ABBREVIATED SYMBOL LEGEND

SYMBOL	HEIGHT	DESCRIPTION
	CEILING	CEILING MOUNTED SPEAKER
	96"	WALL MOUNTED SPEAKER
	AS NOTED	WALL MOUNTED HORN
	48"	VOLUME CONTROL
	48"	PAGING CONSOLE
	FLOOR	PAGING CABINET


DEVICES WITH THE FOLLOWING TAGS ARE AS INDICATED:

- A: EXISTING DEVICES TO REMAIN. PROVIDE NEW CABLING AND CONDUIT AS NEEDED.
- D: EXISTING DEVICES TO BE DEMOLISHED BY THE CONTRACTOR.
- R: EXISTING DEVICES TO BE REPLACED WITH NEW BY THE CONTRACTOR.
- N: NEW DEVICES TO BE PROVIDED AND INSTALLED BY THE CONTRACTOR.

ALL TAGS ARE TO BE NUMBER OF DEVICE UNLESS NOTED OTHERWISE. HEIGHTS INDICATED IN PLANS SHALL SUPERSEDE THOSE IF LISTED HERE.

KEY PLAN


SCALE: NO SCALE

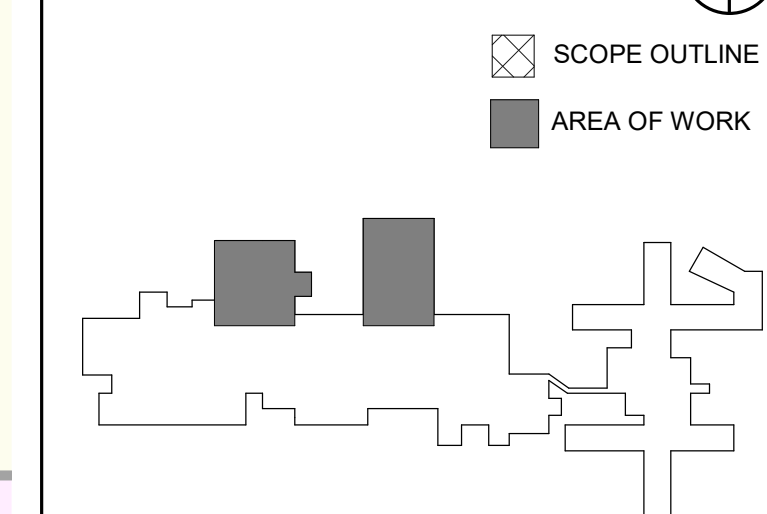


WALL RATING LEGEND

 1 HR - FIRE SEPARATION
 2 HR - FIRE SEPARATION
 SMOKE RESISTIVE HAZARDOUS AREA

FULLY SPRINKLERED
100% CONSTRUCTION DOCUMENTS

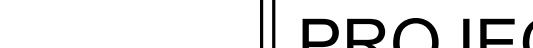			CONSULTANTS:			 			PROJECT MANAGER Headquarters: Apogee Consulting Group, P.A. 1151 Kildaire Farm Road, Suite 120 Cary, North Carolina 27511 www.acg-pa.com 919-858-7420			Office of Construction and Facilities Management VA U.S. Department of Veterans Affairs		Drawing Title BASEMENT FLOOR E PAMNS Location WEST PALM BEACH VAMC 7305 NORTH MILITARY TRAIL WEST PALM BEACH FL, 33410-6400			Project Title REMOVE AND REPLACE PUBLIC ADDRESS SYSTEM Approved Date DECEMBER 14, 2022 Checked JDM Drawn HT			VA PROJECT NUMBER 548-22-100 Building Number # Drawing Number T-104 Dwg 5 of 32	
#	Revisions:	Date																			

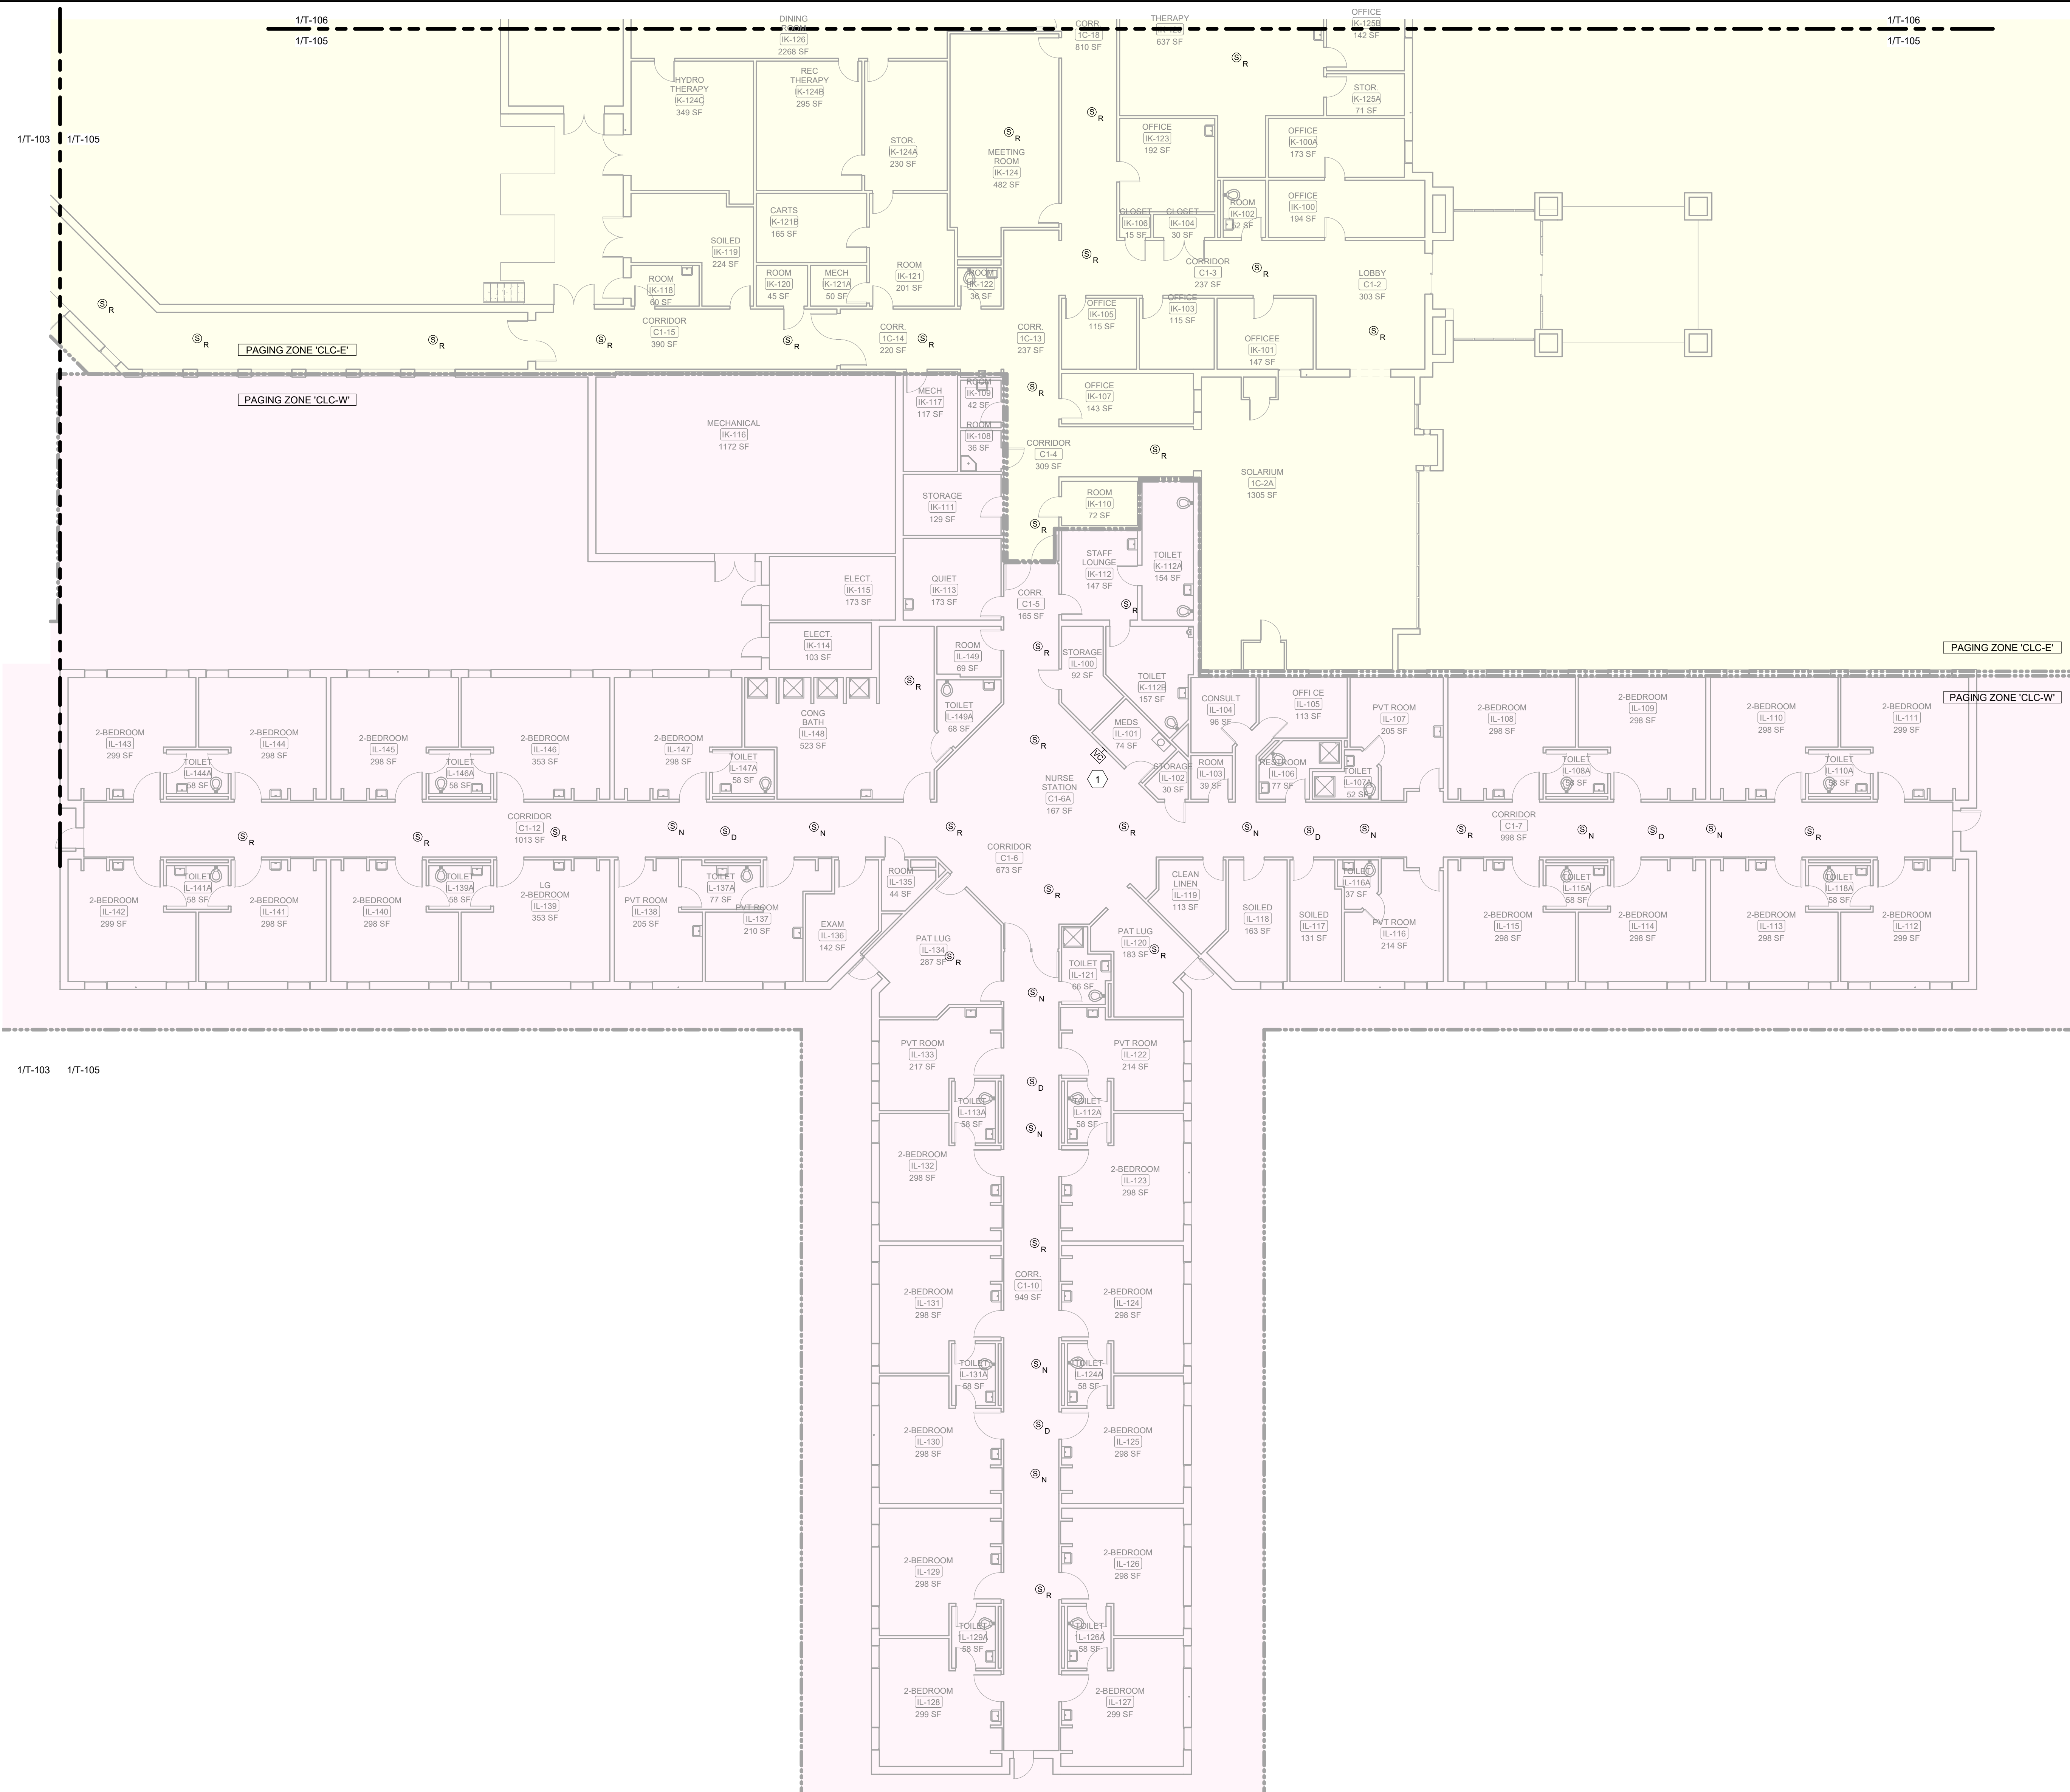

SHEET NOTES:

- A. PROVIDE PAMNS DEVICES AT LOCATIONS INDICATED ON PLANS. PROVIDE WIRING AND CIRCUIT AS INDICATED ON DETAILS.
- B. ALL PAMN WIRING SHALL BE CONCEALED IN WALLS, IN RACEWAY OR ABOVE THE CEILING IN CONDUIT.
- C. PAMN WIRING IN UNFINISHED AREAS SHALL BE IN SURFACE MOUNTED RACEWAY (MECH. ROOM, ROOMS WITH NO CEILINGS.)
- D. ALL CEILING SPEAKERS SHALL BE SET AT 1/2 WALL UNLESS NOTED OTHERWISE.
- E. ALL WALL MOUNTED SPEAKERS SHALL BE SET AT 4 WALLS UNLESS NOTED OTHERWISE.
- F. CONTRACTOR RESPONSIBLE FOR PROVIDING AND INSTALLING FIRE SLEEVES FOR FIREWALL. CONTRACTOR SHALL IMMEDIATELY REPAIR ANY FIREWALL PENETRATIONS.

 KEY NOTES:

- 1 VOLUME TO CONTROL FOR CORRIDOR C1-6,
1 C-SPEAKERS LOCATED IN SPS TO UTILIZE
EXISTING CONDUIT TO PULL SPEAKER
CABLING. SPEAKERS SHALL BE INITIALLY SET
AT 5 WATTS.

ABBREVIATED SYMBOL LEGEND

SYMBOL	HEIGHT	DESCRIPTION
	CEILING	CEILING MOUNTED SPEAKER
	96"	WALL MOUNTED SPEAKER
	AS NOTED	WALL MOUNTED HORN
	48"	VOLUME CONTROL
	48"	PAGING CONSOLE
	FLOOR	PAGING CABINET

DEVICES WITH THE FOLLOWING TAGS ARE AS INDICATED:

C: EXISTING DEVICES TO REMAIN. PROVIDE NEW CABLEING AND CONDUIT AS NEEDED.

D: EXISTING DEVICES TO BE DEMOLISHED BY THE CONTRACTOR.


R: EXISTING DEVICES TO BE REPLACED WITH NEW BY THE CONTRACTOR.

N: NEW DEVICES TO BE PROVIDED AND INSTALLED BY THE CONTRACTOR.


ALL HEIGHTS ARE TO BE THE HEIGHT OF DEVICE UNLESS NOTED OTHERWISE. HEIGHTS INDICATED IN PLANS SHALL SUPERSEDE THOSE LISTED HERE.

KEY PLAN

SCALE: NO SCALE

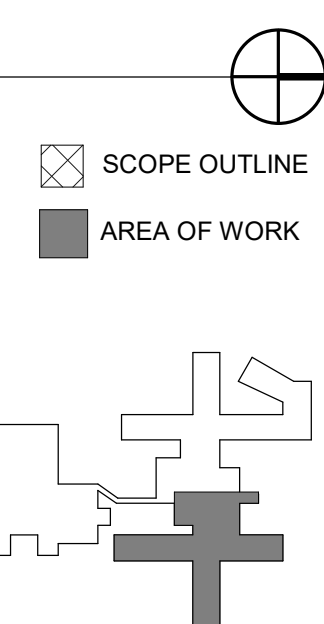



WALL RATING LEGEND

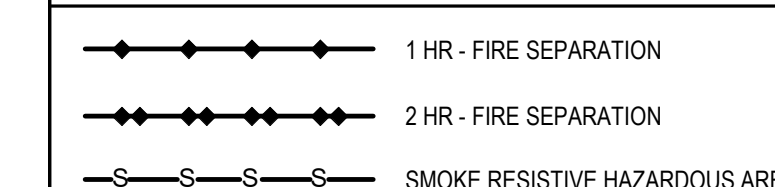

FULLY SPRINKLERED

100% CONSTRUCTION DOCUMENTS

 			CONSULTANTS:			 			PROJECT MANAGER ACG Project Number 22-038			Office of Construction and Facilities Management			Drawing Title CLC NE PAMNS			Project Title REMOVE AND REPLACE PUBLIC ADDRESS SYSTEM			VA PROJECT NUMBER 548-22-100		
									Headquarters: Apogee Consulting Group, P.A. 1151 Kildaire Farm Road, Suite 120 Cary, North Carolina 27511			U.S. Department of Veterans Affairs			Location WEST PALM BEACH VAMC 7305 NORTH MILITARY TRAIL WEST PALM BEACH FL, 33410-6400			Approved Date DECEMBER 14, 2022 Checked JDM Drawn HT			Building Number # Drawing Number T-105		
#	Revisions:	Date				RC04 12/15/2022			www.acg-pa.com 919-858-7420			VA									Dwg 6 of 32		

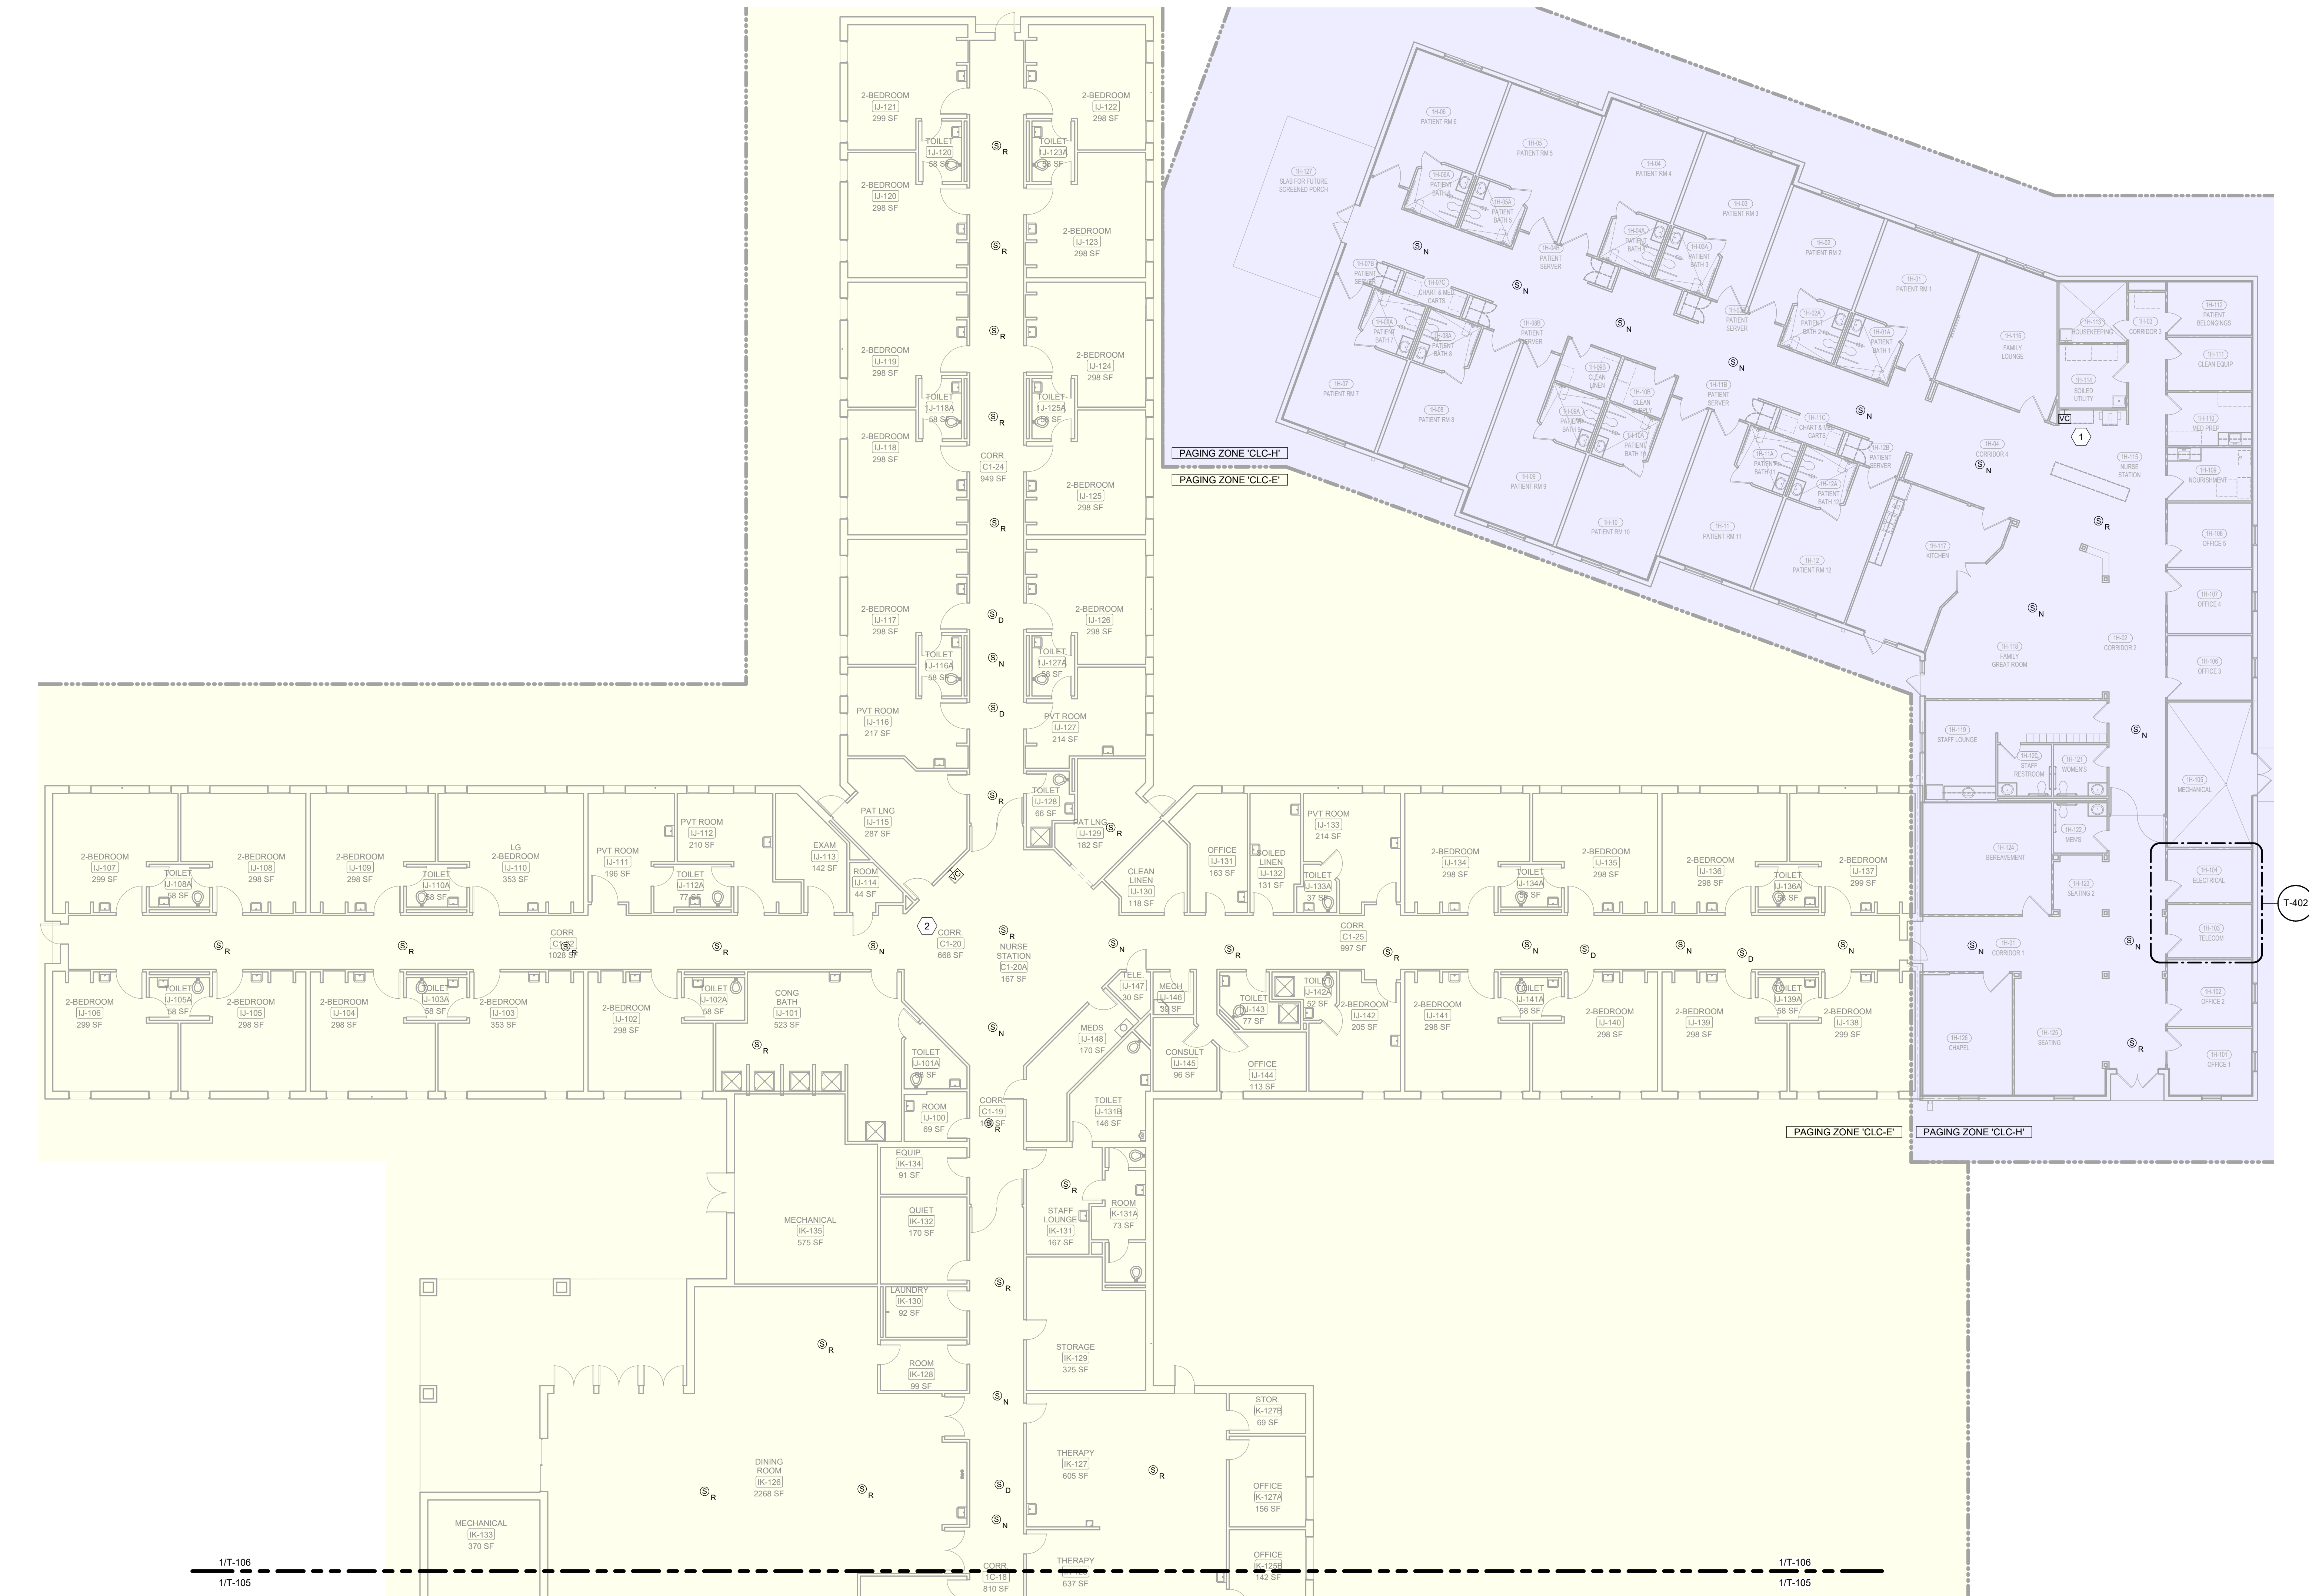

1 CLC SW PAMNS
Scale: 3/32" = 1'-0"

SHEET NOTES:

- PROVIDE PAMNS DEVICES AT LOCATIONS INDICATED ON PLANS. PROVIDE WIRING AND CIRCUIT AS INDICATED ON DETAILS.
- ALL PAMN WIRING SHALL BE CONCEALED IN WALLS, IN RACEWAY OR AND ABOVE THE CEILING IN CONDUIT.
- PAMN WIRING IN UNFINISHED AREAS SHALL BE IN SURFACE MOUNTED RACEWAY (MECH. ROOM, ROOMS WITH NO CEILINGS.)
- ALL CEILING SPEAKERS SHALL BE SET AT 1/2 WATT UNLESS NOTED OTHERWISE.
- ALL WALL MOUNTED SPEAKERS SHALL BE SET AT 4 WATTS UNLESS NOTED OTHERWISE.
- CONTRACTOR RESPONSIBLE FOR PROVIDING AND INSTALLING FIRE SLEEVES FOR FIREWALL. CONTRACTOR SHALL ADEQUATELY REPAIR ANY FIREWALL PENETRATIONS.

KEY NOTES:

- VOLUME CONTROL FOR HOSPICE ZONE CLC-H.
- VOLUME CONTROL FOR CORRIDORS C1-22, C1-24, C1-25.


ABBREVIATED SYMBOL LEGEND

SYMBOL	HEIGHT	DESCRIPTION
Ⓢ	CEILING	CEILING MOUNTED SPEAKER
Ⓢ	96"	WALL MOUNTED SPEAKER
Ⓢ	AS NOTED	WALL MOUNTED HORN
Ⓢ	48"	VOLUME CONTROL
Ⓢ	48"	PAGING CONSOLE
Ⓢ	FLOOR	PAGING CABINET

DEVICES WITH THE FOLLOWING TAGS ARE AS INDICATED:
E: EXISTING DEVICES TO REMAIN. PROVIDE NEW CABLING AND CONDUIT AS NEEDED.
D: EXISTING DEVICES TO BE DEMOLISHED BY THE CONTRACTOR.
R: EXISTING DEVICES TO BE REPLACED WITH NEW BY THE CONTRACTOR.
N: NEW DEVICES TO BE PROVIDED AND INSTALLED BY THE CONTRACTOR.
ALL HEIGHTS ARE TO CENTER OF DEVICE UNLESS NOTED OTHERWISE. HEIGHTS INDICATED IN PLANS SHALL SUPERSEDE THOSE LISTED HERE.

KEY PLAN

SCALE: NO SCALE

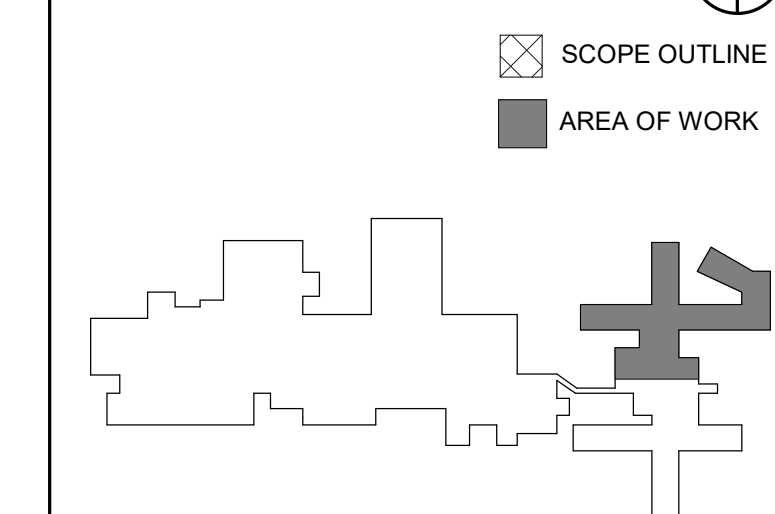

WALL RATING LEGEND


---	1 HR - FIRE SEPARATION
---	2 HR - FIRE SEPARATION
---	SMOKE RESISTIVE HAZARDOUS AREA

FULLY SPRINKLERED
100% CONSTRUCTION DOCUMENTS


--	--	

1-112

Dwg. 9 of 32

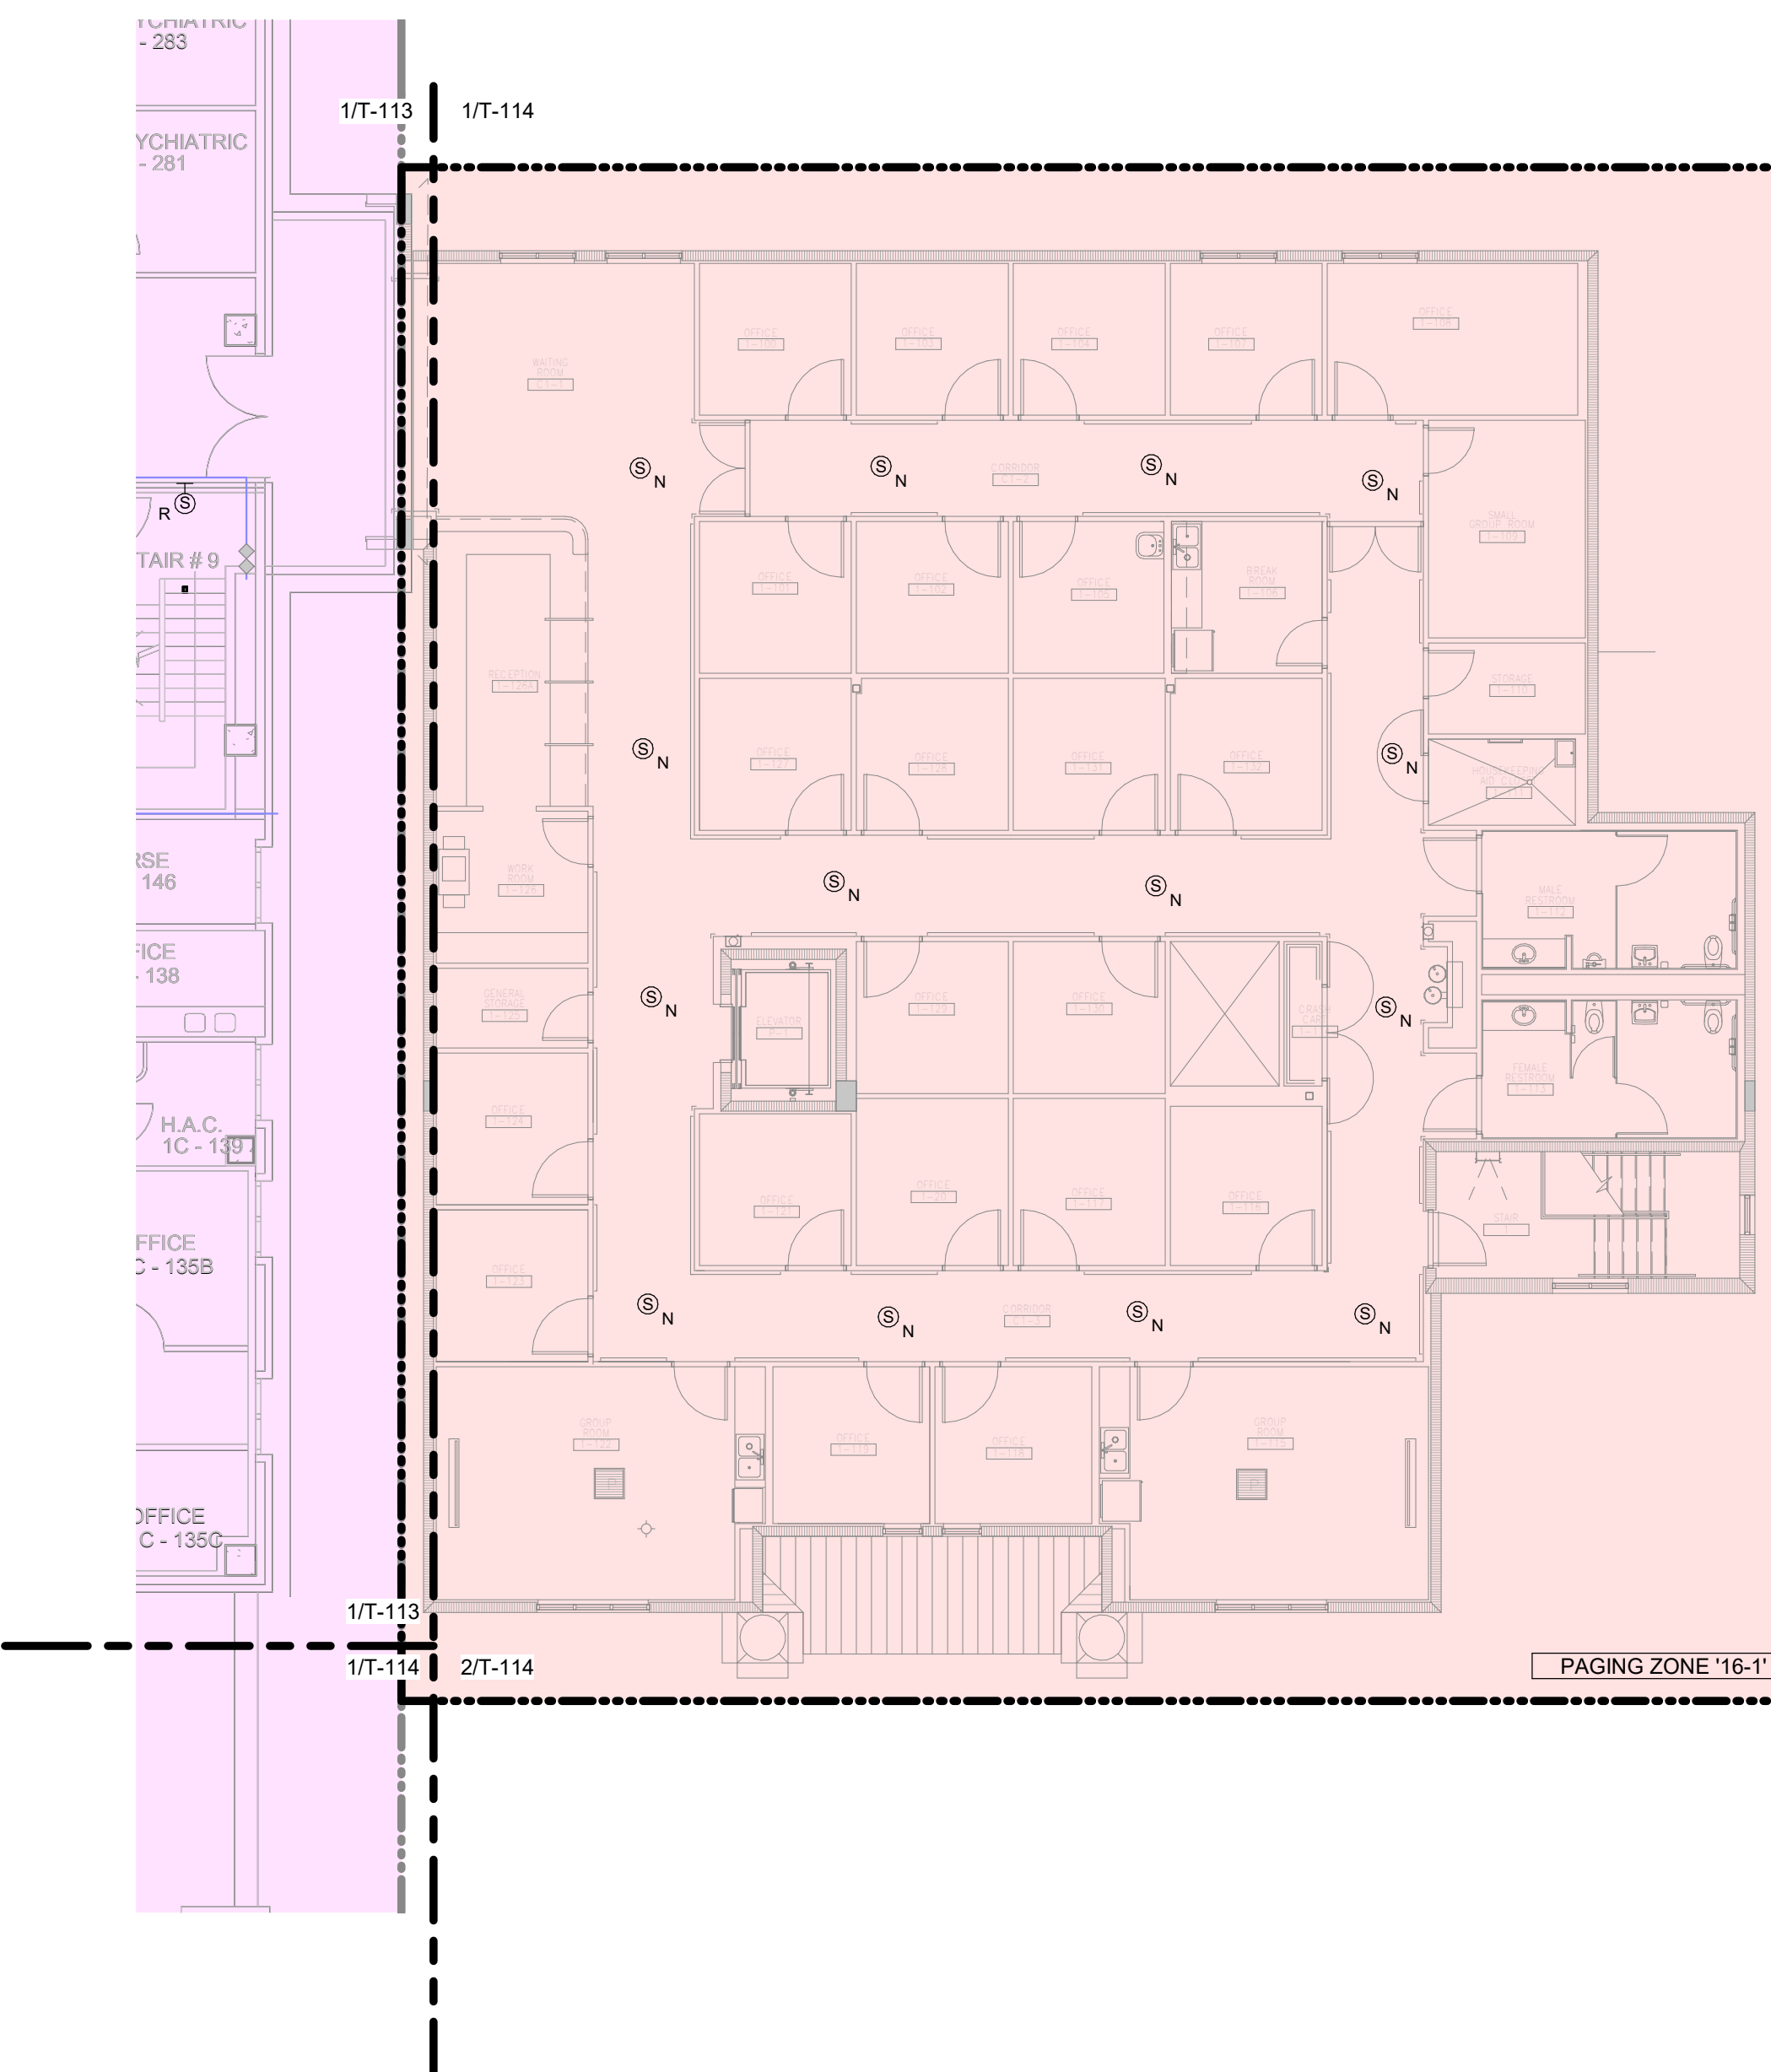

2 BUILDING 16 FIRST FLOOR SE PAMNS
Scale: 3/32" = 1'-0"

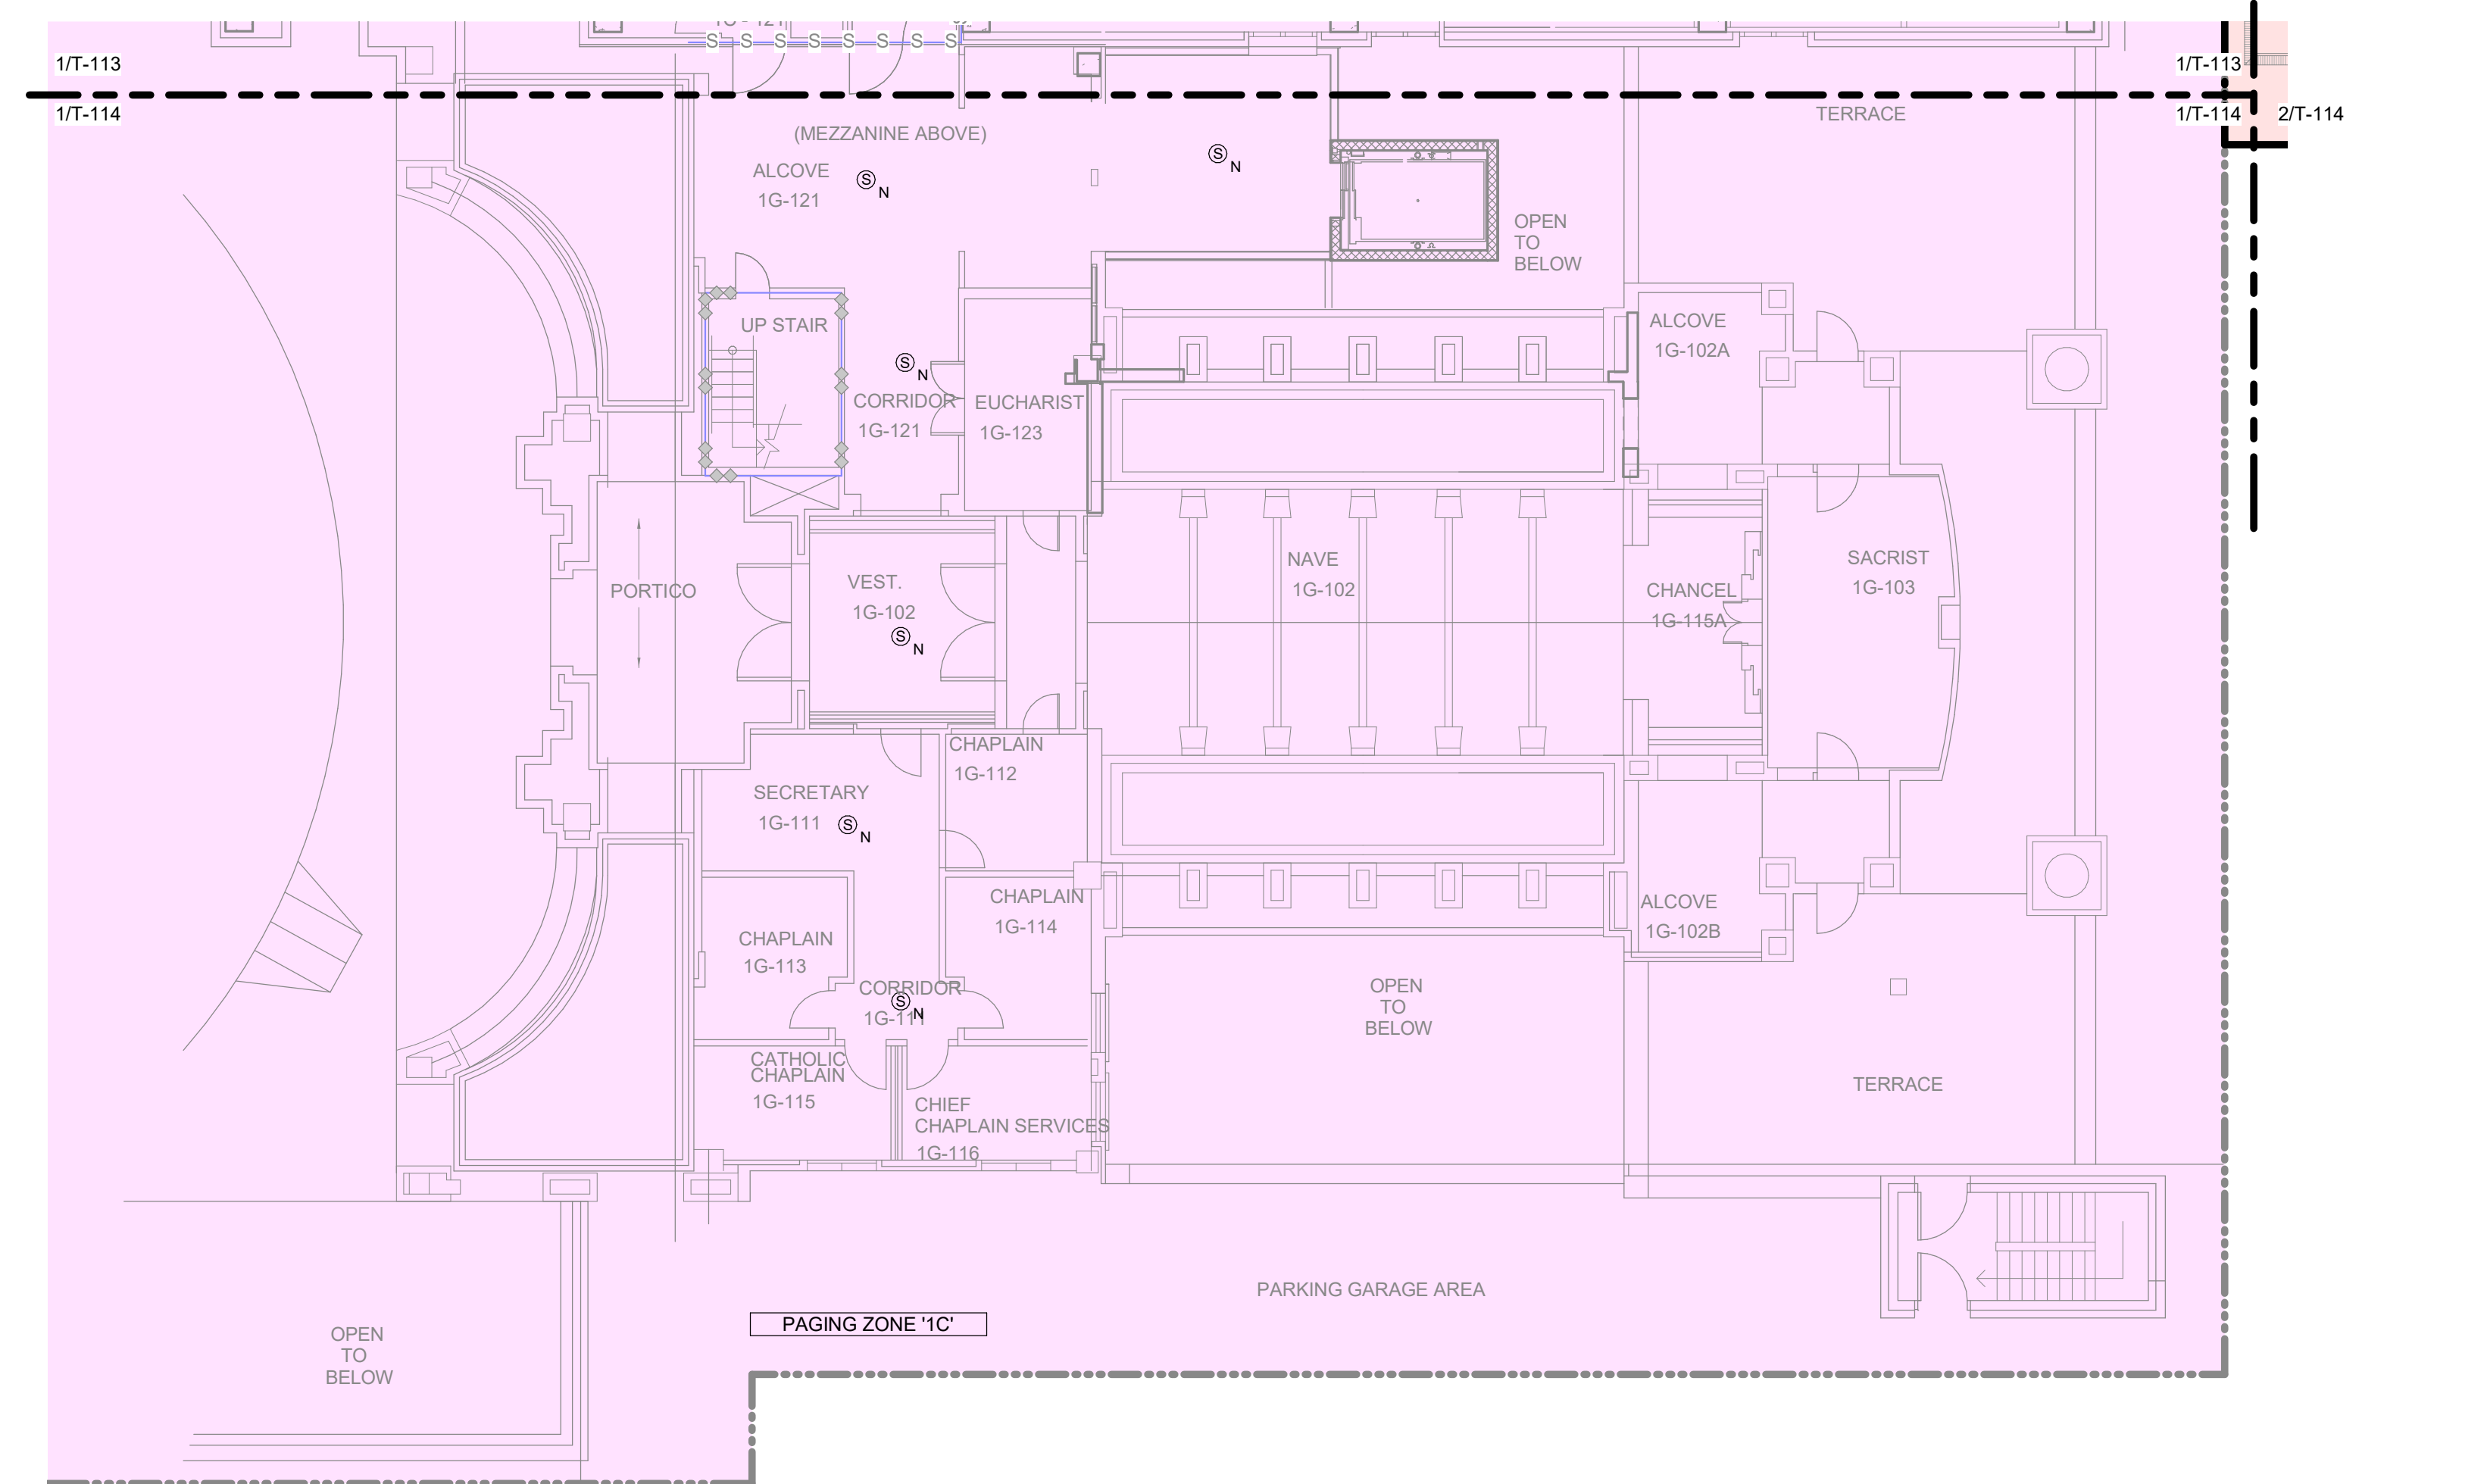

1 FIRST FLOOR E PAMNS
Scale: 3/32" = 1'-0"

SHEET NOTES:

- PROVIDE PAMNS DEVICES AT LOCATIONS INDICATED ON PLANS. PROVIDE WIRING AND CIRCUIT AS INDICATED ON DETAILS.
- ALL PAMN WIRING SHALL BE CONCEALED IN WALLS, IN RACEWAY OR AND ABOVE THE CEILING IN CONDUIT.
- PAMN WIRING IN UNFINISHED AREAS SHALL BE IN SURFACE MOUNTED RACEWAY (MECH. ROOM, ROOMS WITH NO CEILINGS.)
- ALL CEILING SPEAKERS SHALL BE SET AT 1/2 WATT UNLESS NOTED OTHERWISE.
- ALL WALL MOUNTED SPEAKERS SHALL BE SET AT 4 WATTS UNLESS NOTED OTHERWISE.
- CONTRACTOR RESPONSIBLE FOR PROVIDING AND INSTALLING FIRE SLEEVES FOR FIREWALL. CONTRACTOR SHALL ADEQUATELY REPAIR ANY FIREWALL PENETRATIONS.

#

KEY NOTES:


ABBREVIATED SYMBOL LEGEND

SYMBOL	HEIGHT	DESCRIPTION
Ⓢ	CEILING	CEILING MOUNTED SPEAKER
Ⓢ	96"	WALL MOUNTED SPEAKER
Ⓢ	AS NOTED	WALL MOUNTED HORN
Ⓢ	48"	VOLUME CONTROL
Ⓢ	48"	PAGING CONSOLE
Ⓢ	FLOOR	PAGING CABINET


DEVICES WITH THE FOLLOWING TAGS ARE AS INDICATED:
E: EXISTING DEVICES TO REMAIN. PROVIDE NEW CABLING AND CONDUIT AS NEEDED.
D: EXISTING DEVICES TO BE DEMOLISHED BY THE CONTRACTOR.
R: EXISTING DEVICES TO BE REPLACED WITH NEW BY THE CONTRACTOR.
N: NEW DEVICES TO BE PROVIDED AND INSTALLED BY THE CONTRACTOR.
ALL HEIGHTS ARE TO CENTER OF DEVICE UNLESS NOTED OTHERWISE. HEIGHTS INDICATED IN PLANS SHALL SUPERSEDE THOSE LISTED HERE.

KEY PLAN

SCALE: NO SCALE

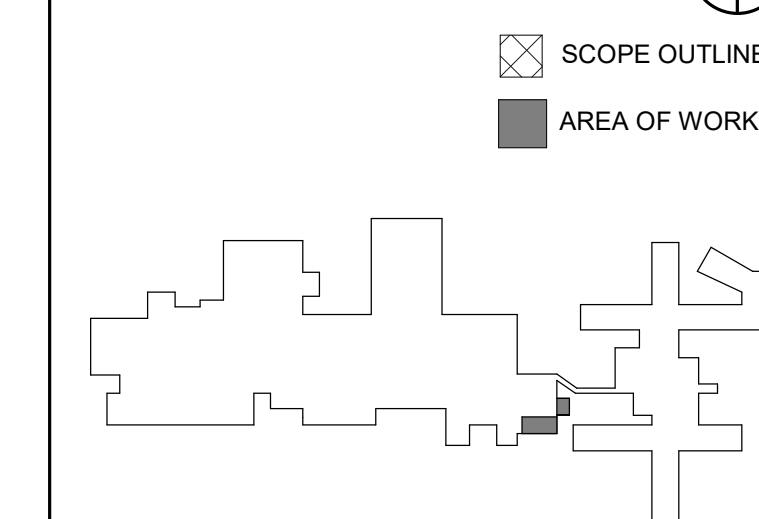


WALL RATING LEGEND

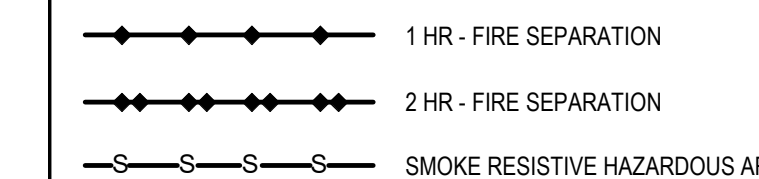


FULLY SPRINKLERED 100% CONSTRUCTION DOCUMENTS

	</
--	--	----

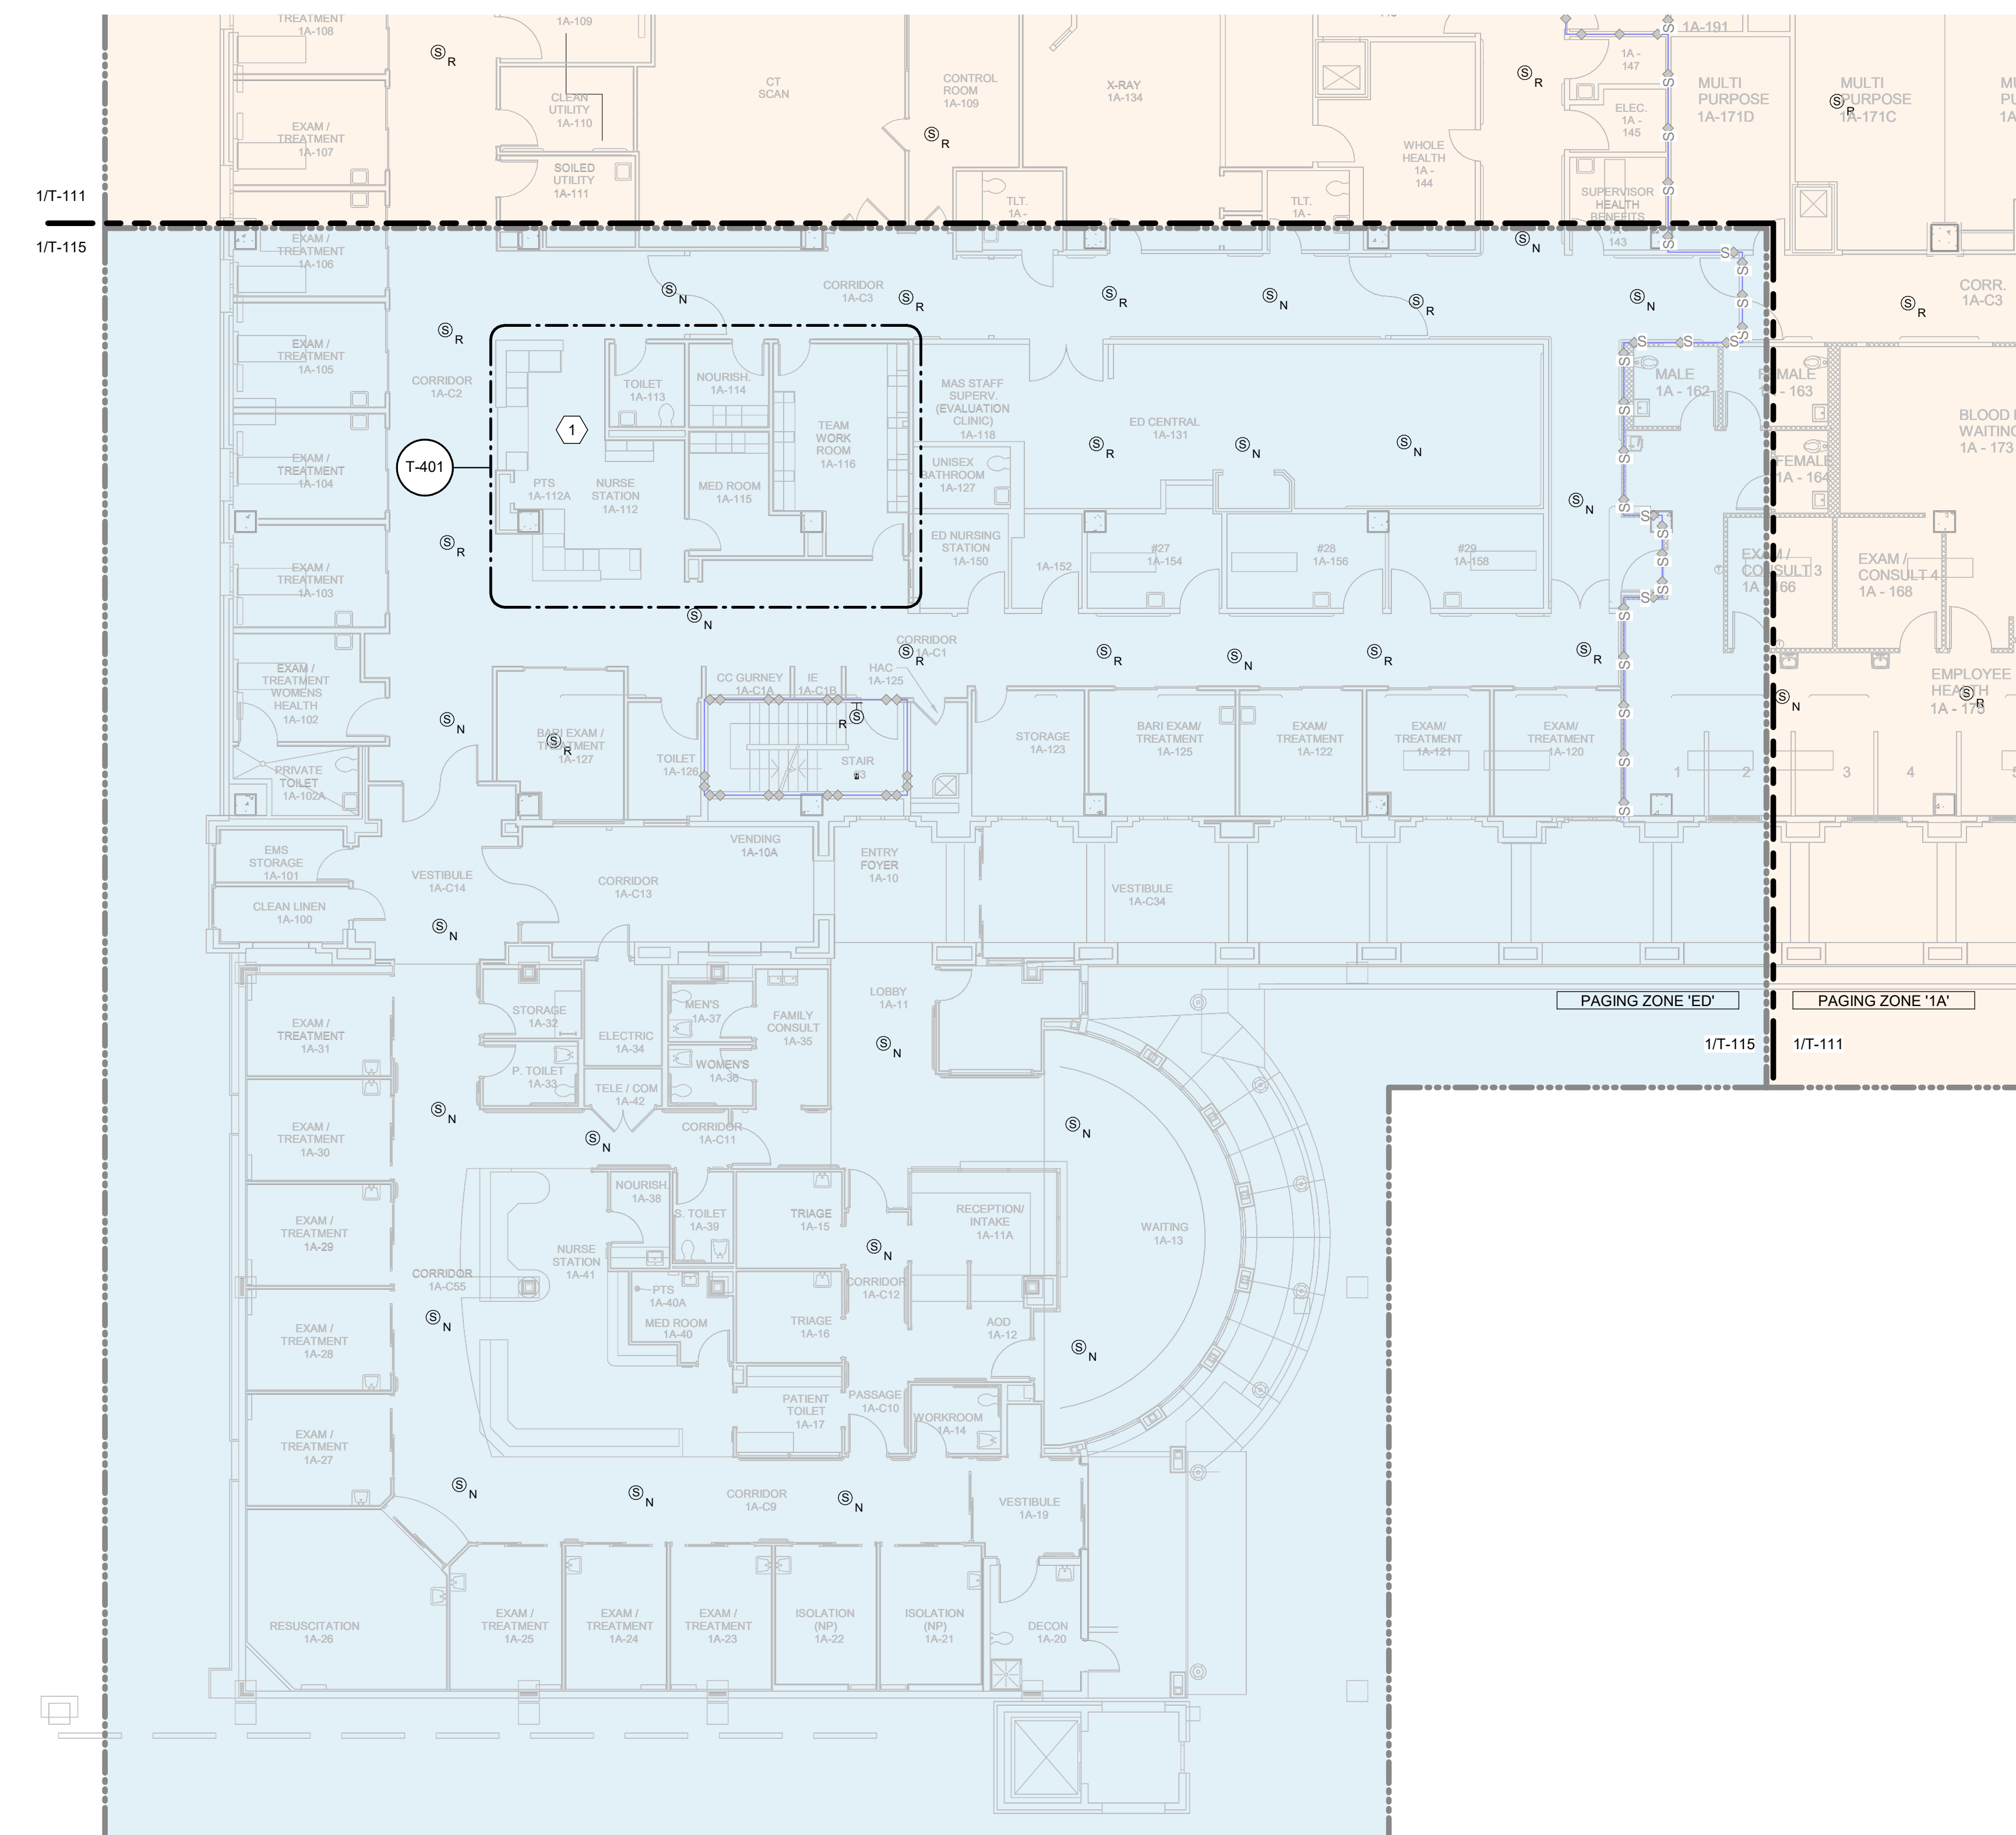

1 FIRST FLOOR S PAMN
Scale: 3/32" = 1'-0"

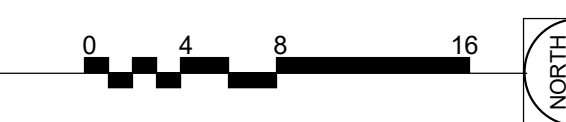

SHEET NOTES:

- A. PROVIDE PAMMS DEVICES AT LOCATIONS INDICATED ON PLANS. PROVIDE WIRING AND CIRCUIT AS INDICATED ON DETAILS.
- B. ALL PAMM WIRING SHALL BE CONCEALED IN WALL, IN RACEWAY, OR ABOVE THE CEILING IN CONDUIT.
- C. PAMM WIRING IN UNFINISHED AREAS SHALL BE IN SURFACE MOUNTED RACEWAY (MECH. ROOM, ROOMS WITH NO CEILINGS.)
- D. ALL CEILING SPEAKERS SHALL BE SET AT 1/2 WALL UNLESS NOTED OTHERWISE.
- E. ALL WALL MOUNTED SPEAKERS SHALL BE SET AT 4 WALLS UNLESS NOTED OTHERWISE.
- F. CONTRACTOR RESPONSIBLE FOR PROVIDING AND INSTALLING FIRE SLEEVES FOR FIREWALL. CONTRACTOR SHALL IMMEDIATELY REPAIR ANY FIREWALL PENETRATIONS.

 KEY NOTES:

- 1 VOLUME CONTROL FOR EMERGENCY ROOM
1A-C3, 1A-C14, 1A-C13, 1A-C1, 1A-109.

**ABBREVIATED SYMBOL
LEGEND**

SYMBOL	HEIGHT	DESCRIPTION
	CEILING	CEILING MOUNTED SPEAKER
	96"	WALL MOUNTED SPEAKER
	AS NOTED	WALL MOUNTED HORN
	48"	VOLUME CONTROL
	48"	PAGING CONSOLE
	FLOOR	PAGING CABINET


DEVICES WITH THE FOLLOWING TAGS ARE AS INDICATED: C: EXISTING DEVICES TO REMAIN. PROVIDE NEW CABLING AND CONDUIT AS NEEDED. D: EXISTING DEVICES TO BE DEMOLISHED BY THE CONTRACTOR. R: EXISTING DEVICES TO BE REPLACED WITH NEW BY THE CONTRACTOR. N: NEW DEVICES TO BE PROVIDED AND INSTALLED BY THE CONTRACTOR. ALL HEIGHTS ARE TO BE IN FEET OF DEVICE UNLESS NOTED OTHERWISE. HEIGHTS INDICATED IN PLANS SHALL SUPERSEDE THOSE LISTED HERE.

KEY PLAN

SCALE: NO SCALE

 **SCORE OUTLINE**

 SCOPE OUTLINE

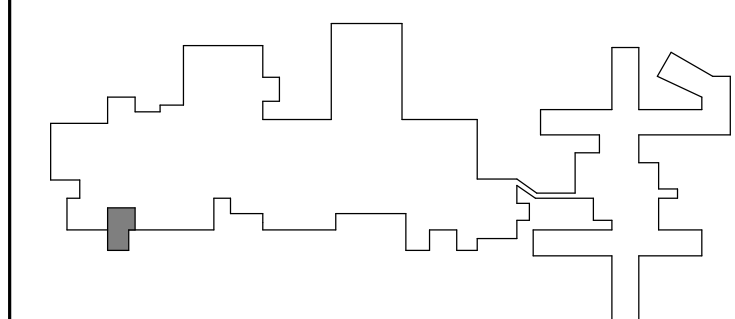

WALL RATING LEGEND


1 HR - FIRE SEPARATION

2 HR - FIRE SEPARATION

SMOKE RESISTIVE HAZARDOUS AREA

FULLY SPRINKLERED
100% CONSTRUCTION DOCUMENTS

	</
--	--	----

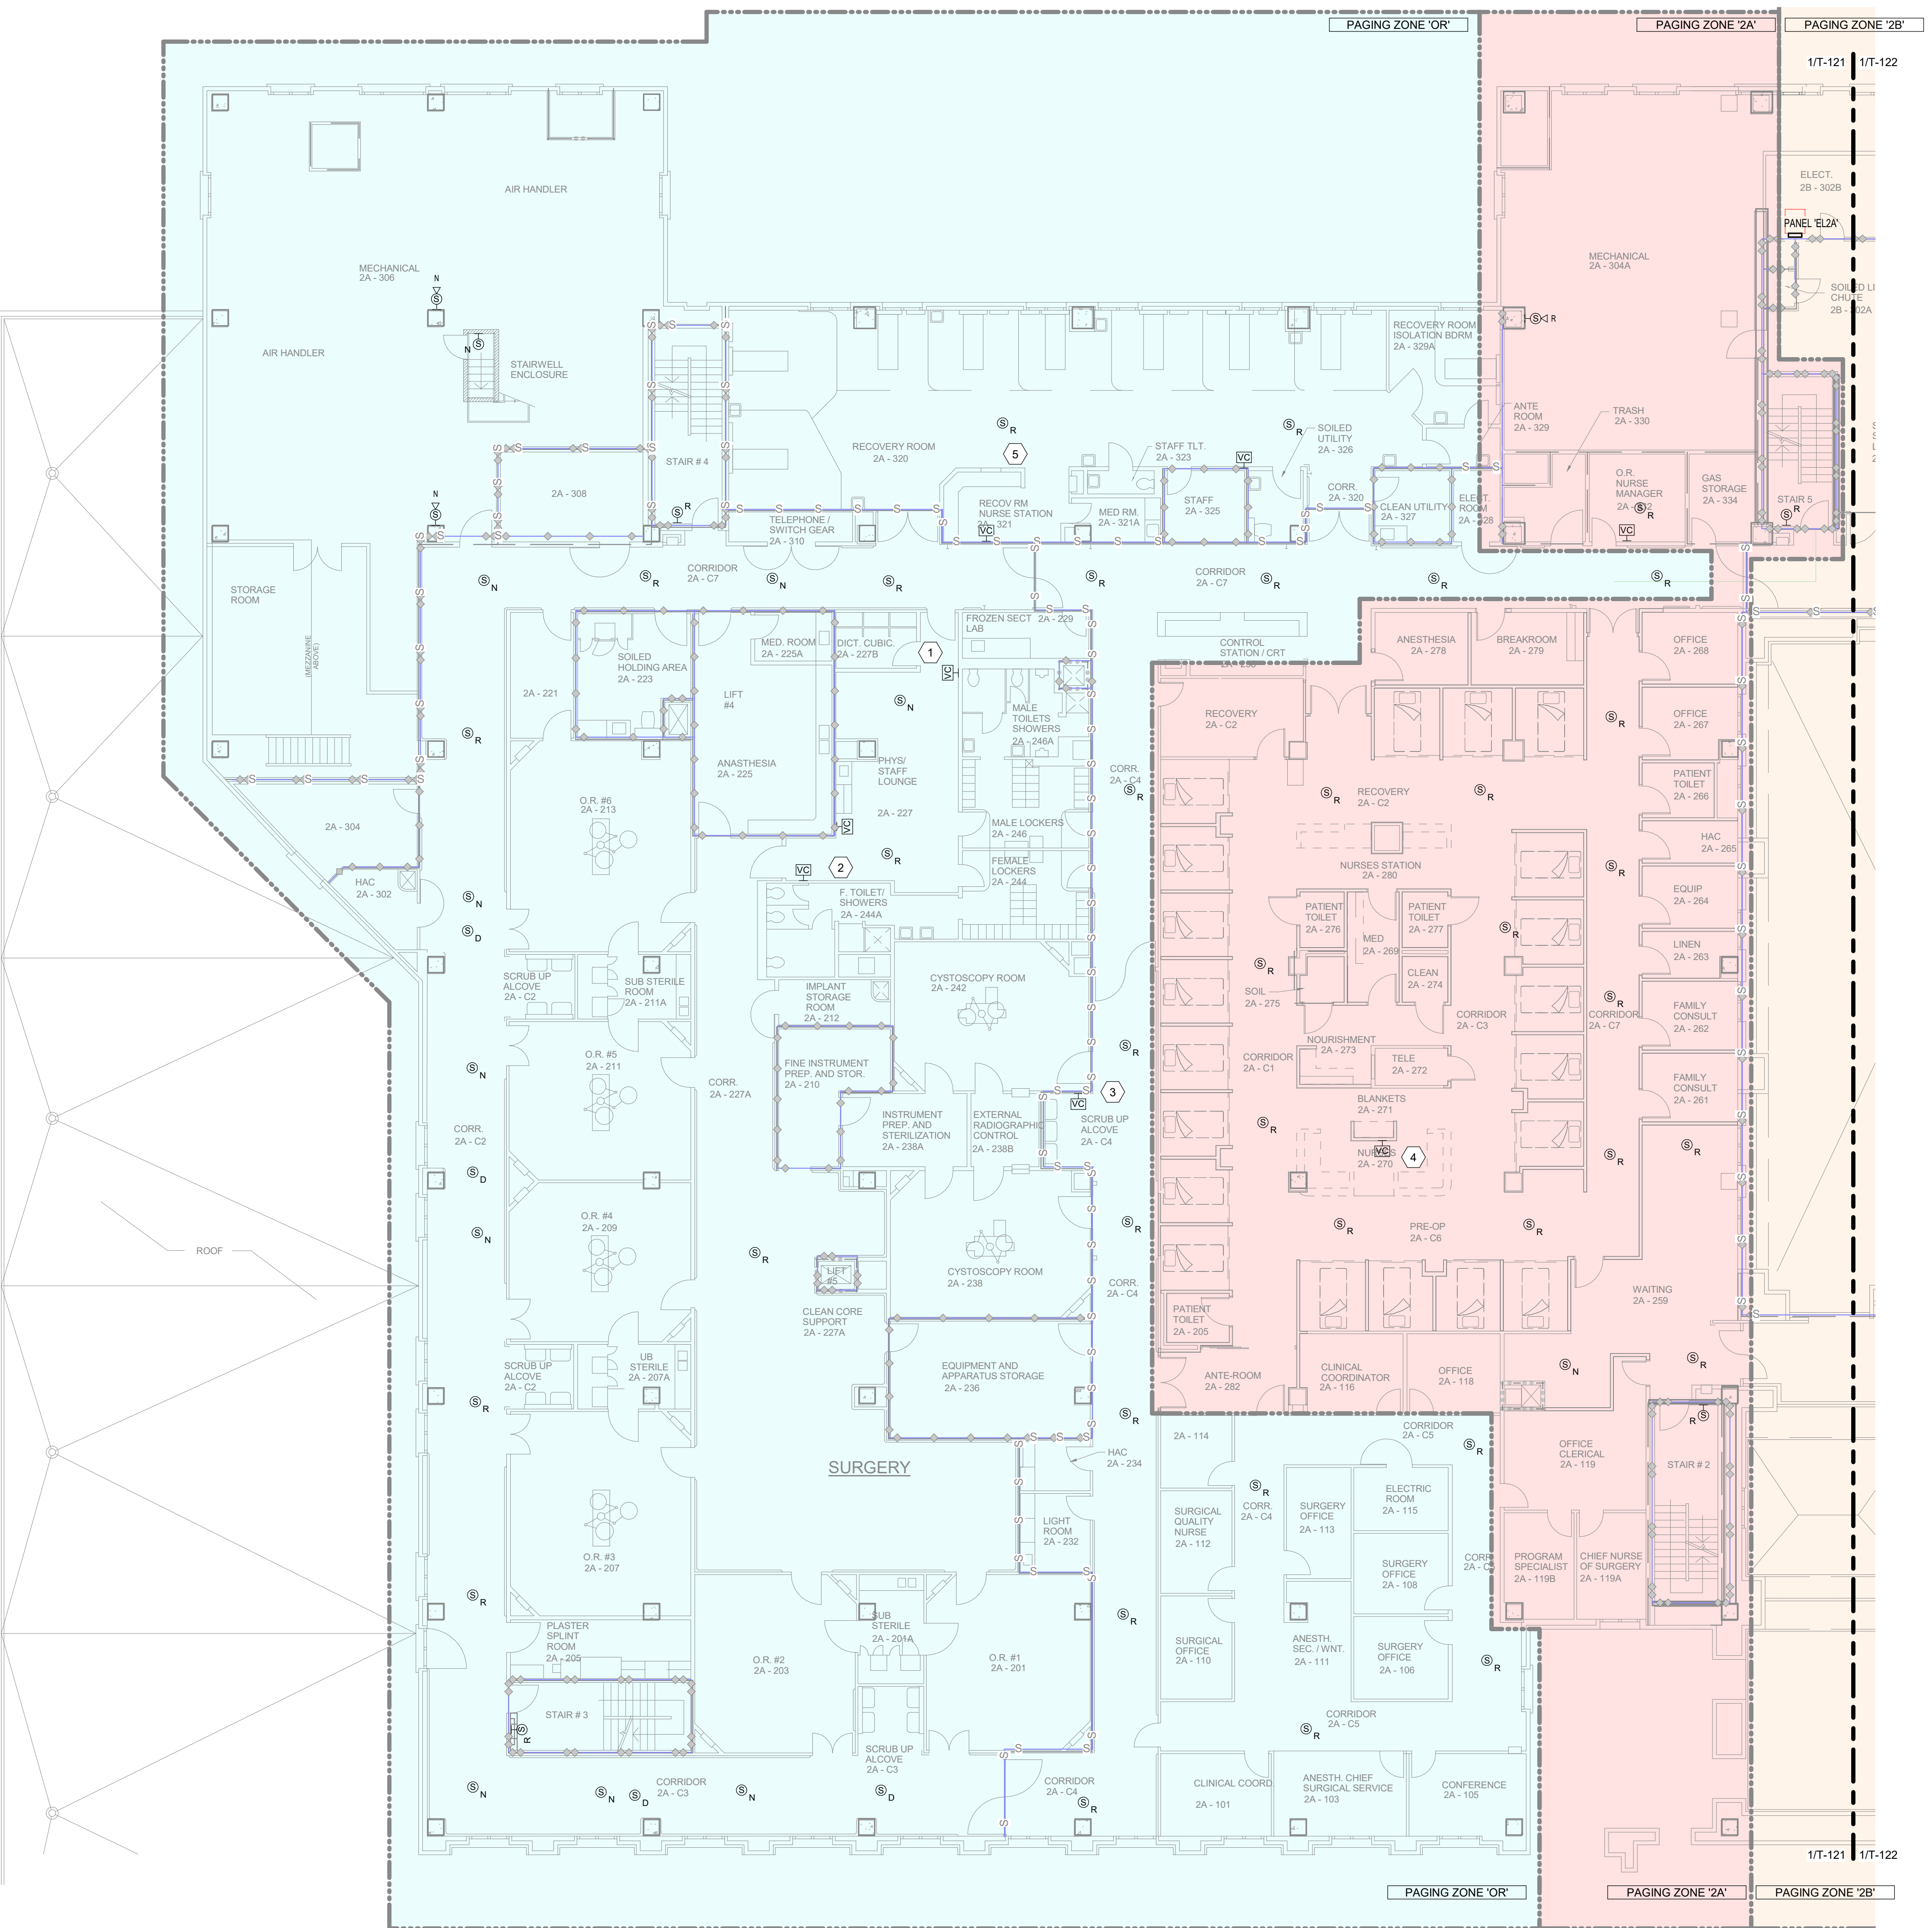

SHEET NOTES:

- A. PROVIDE PAMNS DEVICES AT LOCATIONS INDICATED ON PLANS. PROVIDE WIRING AND CIRCUIT AS INDICATED ON DETAILS.
- B. ALL PAMN WIRING SHALL BE CONCEALED IN WALLS, IN RACEWAY OR AND ABOVE THE CEILING IN CONDUIT.
- C. PAMN WIRING IN UNFINISHED AREAS SHALL BE IN SURFACE MOUNTED RACEWAY (MECH. ROOM, ROOMS WITH NO CEILINGS.)
- D. ALL CEILING SPEAKERS SHALL BE SET AT 1/2 WATT UNLESS NOTED OTHERWISE.
- E. ALL WALL MOUNTED SPEAKERS SHALL BE SET AT 4 WATTS UNLESS NOTED OTHERWISE.
- F. CONTRACTOR RESPONSIBLE FOR PROVIDING AND INSTALLING FIRE SLEEVES FOR FIREWALL. CONTRACTOR SHALL ADEQUATELY REPAIR ANY FIREWALL PENETRATIONS.

#

KEY NOTES:

- 1 VOLUME CONTROL FOR SURGICAL CORRIDORS 2A-C2, 2A-C3, 2A-C7
- 2 VOLUME CONTROL FOR STERILE CORE 2A-227A
- 3 VOLUME CONTROL FOR CORRIDORS 2A-C4
- 4 VOLUME CONTROL FOR ANTEROOM 2A-282 & PREOP/RECOVERY 2A-C1, 2A-C2, 2A-C3, 2A-C6, 2A-C7
- 5 VOLUME CONTROL FOR RECOVERY ROOM 2A-320


ABBREVIATED SYMBOL LEGEND

SYMBOL	HEIGHT	DESCRIPTION
Ⓢ	CEILING	CEILING MOUNTED SPEAKER
Ⓢ	96"	WALL MOUNTED SPEAKER
Ⓢ	AS NOTED	WALL MOUNTED HORN
Ⓢ	48"	VOLUME CONTROL
Ⓢ	48"	PAGING CONSOLE
Ⓢ	FLOOR	PAGING CABINET

DEVICES WITH THE FOLLOWING TAGS ARE AS INDICATED:
E: EXISTING DEVICES TO REMAIN. PROVIDE NEW CABLING AND CONDUIT AS NEEDED.
D: EXISTING DEVICES TO BE DEMOLISHED BY THE CONTRACTOR.
R: EXISTING DEVICES TO BE REPLACED WITH NEW BY THE CONTRACTOR.
N: NEW DEVICES TO BE PROVIDED AND INSTALLED BY THE CONTRACTOR.
ALL HEIGHTS ARE TO CENTER OF DEVICE UNLESS NOTED OTHERWISE. HEIGHTS INDICATED IN PLANS SHALL SUPERSEDE THOSE LISTED HERE.

KEY PLAN

SCALE: NO SCALE

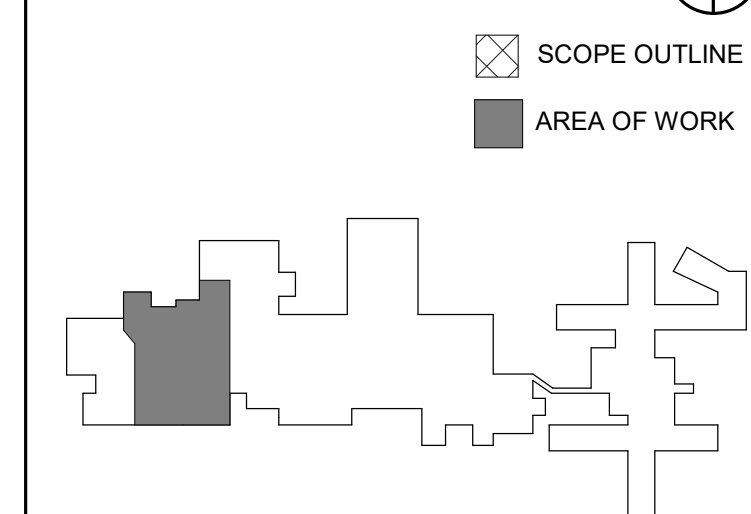

WALL RATING LEGEND

- 1 HR - FIRE SEPARATION
- 2 HR - FIRE SEPARATION
- SMOKE RESISTIVE HAZARDOUS AREA



FULLY SPRINKLERED

100% CONSTRUCTION DOCUMENTS

1 SECOND FLOOR SE PAMNS

Scale: 3/32" = 1'-0"

CONSULTANTS:

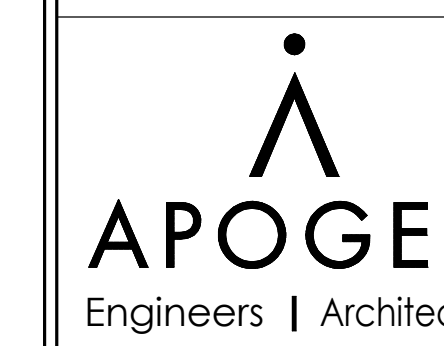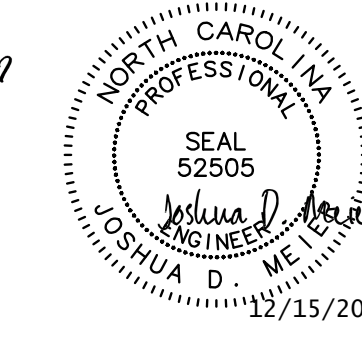

PROJECT MANAGER
Headquarters:
Apogee Consulting Group, P.A.
1151 Kildaire Farm Road, Suite 120
Cary, North Carolina 27511

Office of
Construction
and Facilities
Management


U.S. Department
of Veterans Affairs

Drawing Title
SECOND FLOOR SE PAMNS
Location
**WEST PALM BEACH VAMC
7305 NORTH MILITARY TRAIL
WEST PALM BEACH FL, 33410-6400**

Project Title
**REMOVE AND REPLACE
PUBLIC ADDRESS SYSTEM**
Approved
Date
DECEMBER 14, 2022

VA PROJECT NUMBER
548-22-100
Building Number

Drawing Number
T-121
Dwg 13 of 32

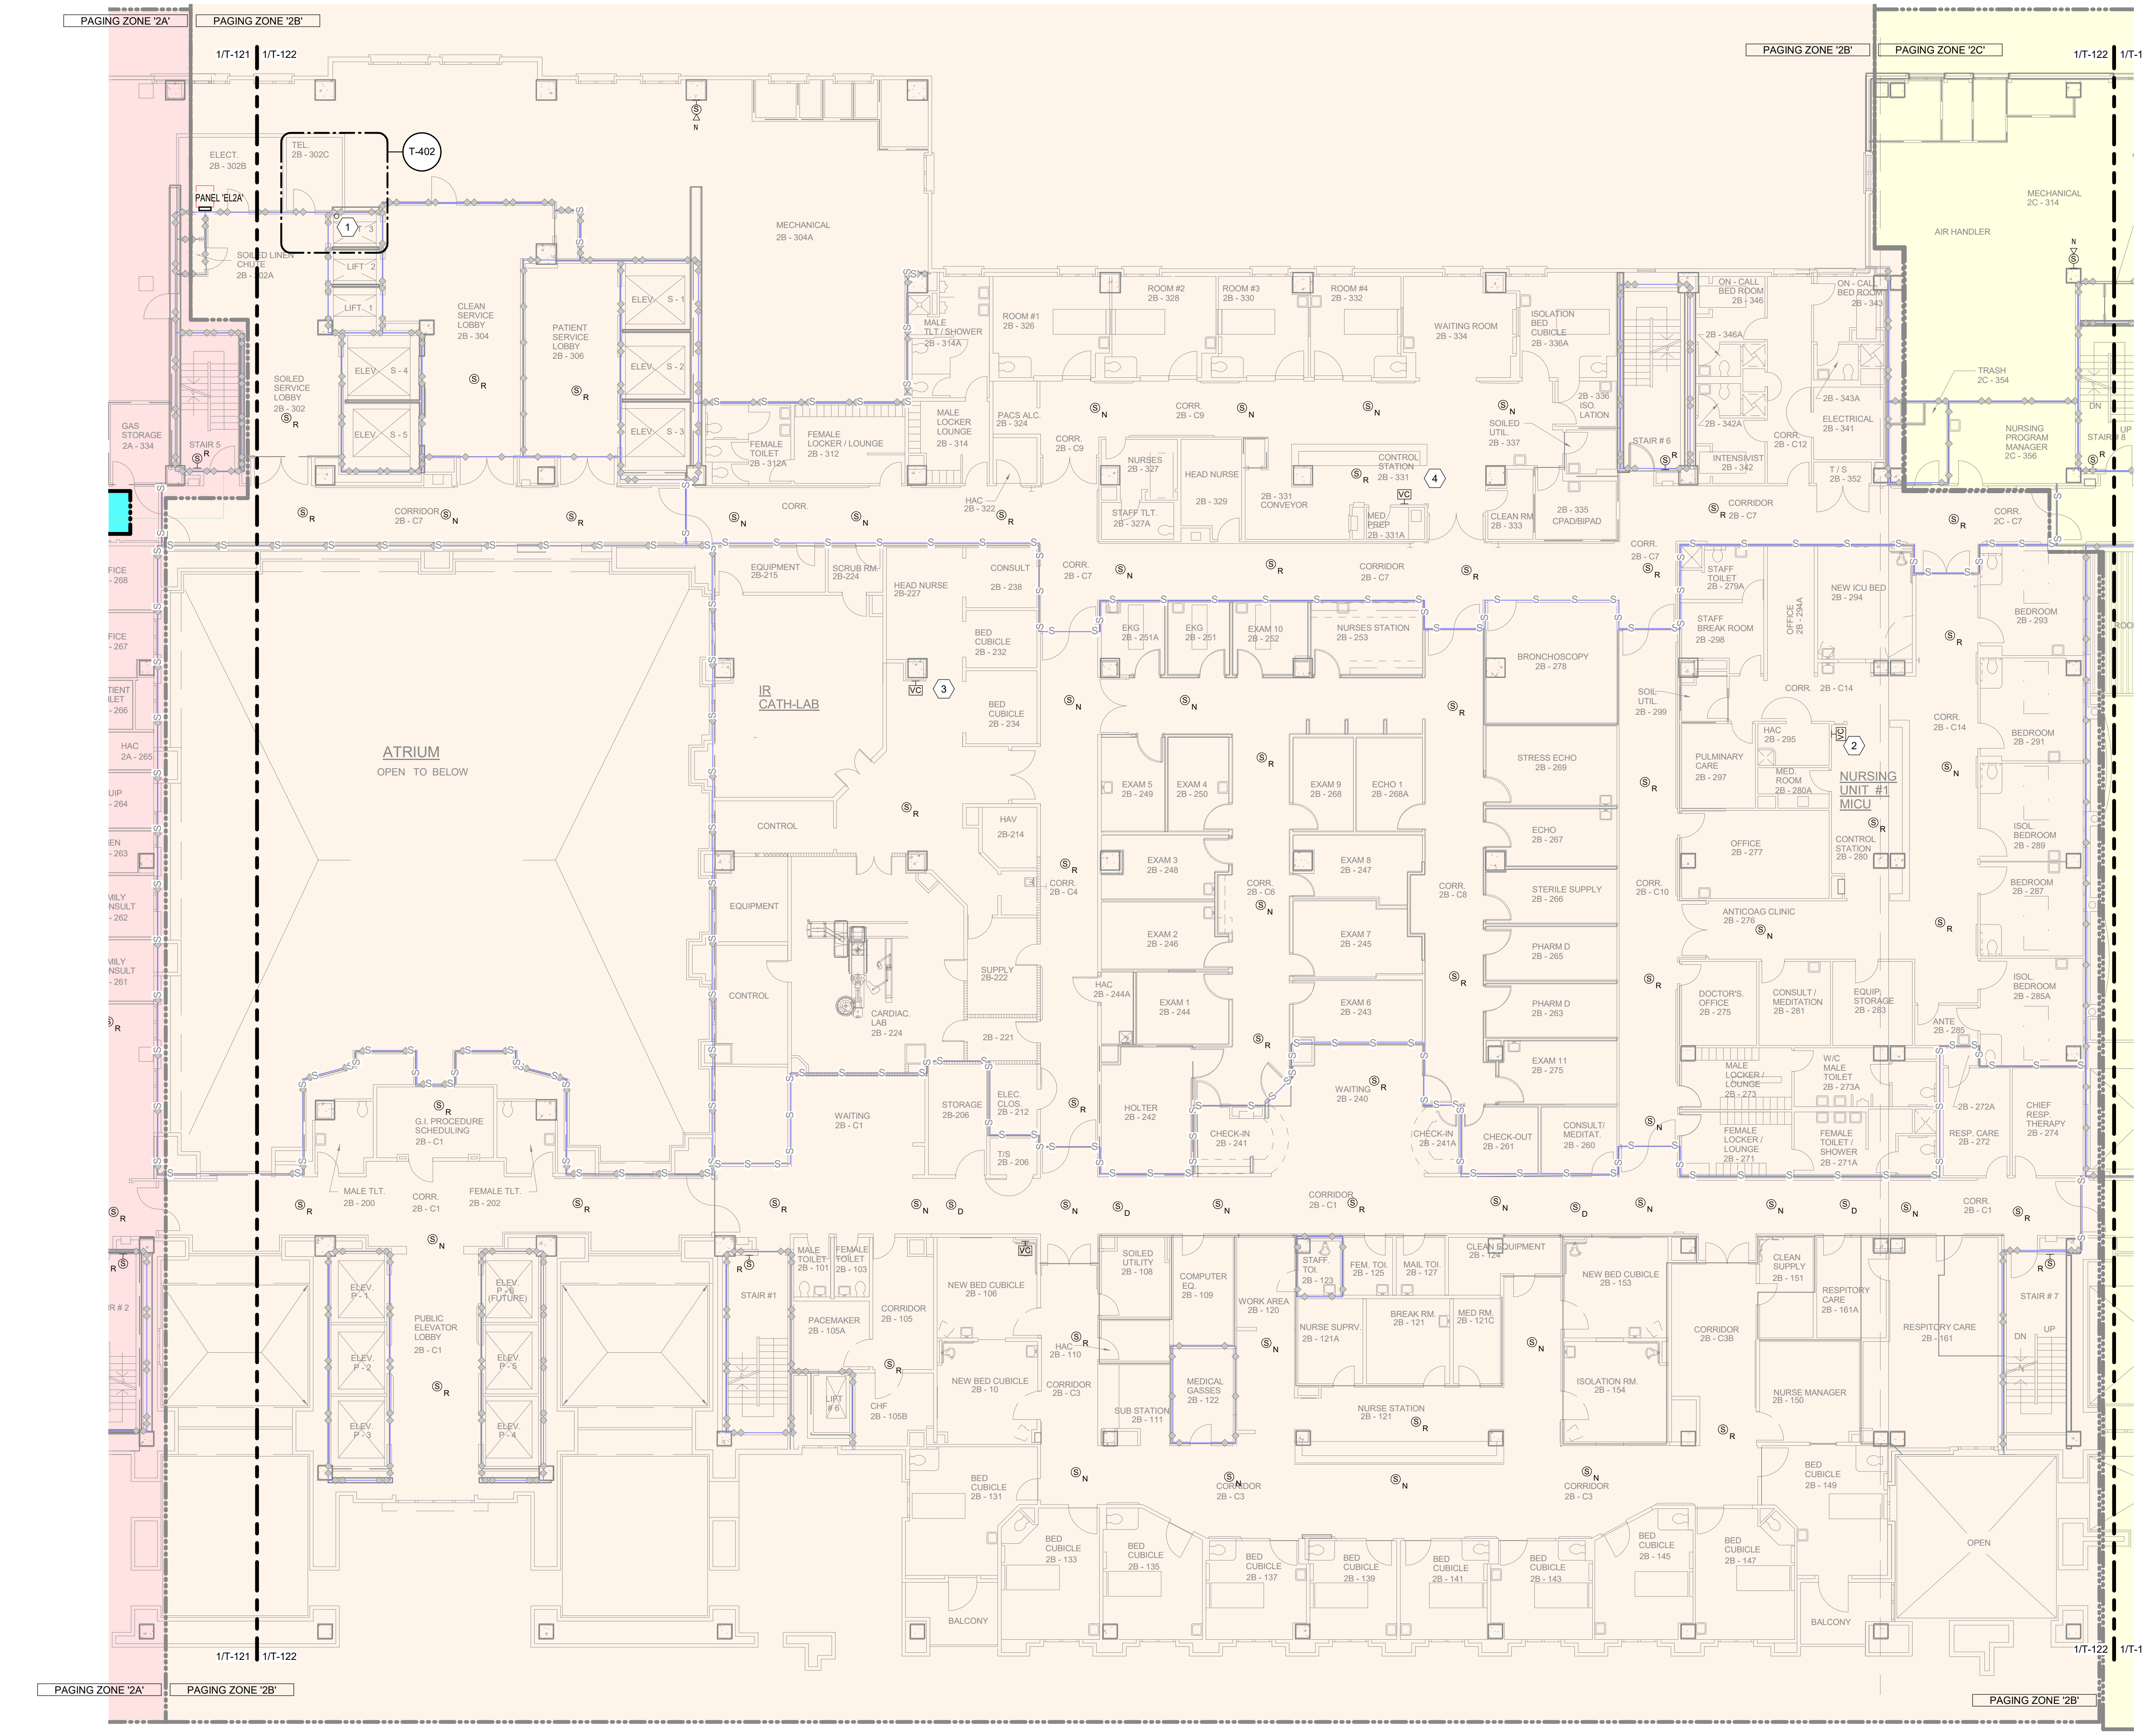

1 SECOND FLOOR CENT PAMNS
Scale: 3/32" = 1'-0"

SHEET NOTES:

- A. PROVIDE PAMNS DEVICES AT LOCATIONS INDICATED ON PLANS. PROVIDE WIRING AND CIRCUIT AS INDICATED ON DETAILS.
- B. ALL PAMN WIRING SHALL BE CONCEALED IN WALLS, IN RACEWAY OR AND ABOVE THE CEILING IN CONDUIT.
- C. PAMN WIRING IN UNFINISHED AREAS SHALL BE IN SURFACE MOUNTED RACEWAY (MECH. ROOM, ROOMS WITH NO CEILINGS.)
- D. ALL CEILING SPEAKERS SHALL BE SET AT 1/2 WATT UNLESS NOTED OTHERWISE.
- E. ALL WALL MOUNTED SPEAKERS SHALL BE SET AT 4 WATTS UNLESS NOTED OTHERWISE.
- F. CONTRACTOR RESPONSIBLE FOR PROVIDING AND INSTALLING FIRE SLEEVES FOR FIREWALL. CONTRACTOR SHALL ADEQUATELY REPAIR ANY FIREWALL PENETRATIONS.

KEY NOTES:

- 1 LOCATION OF VERTICAL RISER IN LIFT SHAFT. REF. T-601
- 2 VOLUME CONTROL FOR MICU CORRIDORS 2B-C14, 2B-276, 2B-280, AND 2B-294A.
- 3 VOLUME CONTROL FOR CATH 2B-227 AND CATH LAB CORRIDORS.
- 4 VOLUME CONTROL FOR ICU 2B-C9, 2B-331, AND 2B-334.

ABBREVIATED SYMBOL LEGEND

SYMBOL	HEIGHT	DESCRIPTION
Ⓢ	CEILING	CEILING MOUNTED SPEAKER
Ⓢ 96"	96"	WALL MOUNTED SPEAKER
Ⓢ NOTED	AS NOTED	WALL MOUNTED HORN
Ⓢ 48"	48"	VOLUME CONTROL
Ⓢ 48"	48"	PAGING CONSOLE
Ⓢ PA	FLOOR	PAGING CABINET

DEVICES WITH THE FOLLOWING TAGS ARE AS INDICATED:
E: EXISTING DEVICES TO REMAIN. PROVIDE NEW CABLING AND CONDUIT AS NEEDED.
D: EXISTING DEVICES TO BE DEMOLISHED BY THE CONTRACTOR.
R: EXISTING DEVICES TO BE REPLACED WITH NEW BY THE CONTRACTOR.
N: NEW DEVICES TO BE PROVIDED AND INSTALLED BY THE CONTRACTOR.
ALL HEIGHTS ARE TO CENTER OF DEVICE UNLESS NOTED OTHERWISE. HEIGHTS INDICATED IN PLANS SHALL SUPERSEDE THOSE LISTED HERE.

KEY PLAN

SCALE: NO SCALE


SCOPE OUTLINE
AREA OF WORK

WALL RATING LEGEND


- 1 HR - FIRE SEPARATION
- 2 HR - FIRE SEPARATION
- SMOKE RESISTIVE HAZARDOUS AREA

FULLY SPRINKLERED
100% CONSTRUCTION DOCUMENTS

CONSULTANTS:		PROJECT MANAGER ACG Project Number 22-038 APOGEE Headquarters: Apogee Consulting Group, P.A. 1151 Kildaire Farm Road, Suite 120 Cary, North Carolina 27511 www.acg-pa.com 919-858-7420		Office of Construction and Facilities Management U.S. Department of Veterans Affairs		Drawing Title SECOND FLOOR CENT PAMNS Location WEST PALM BEACH VAMC 7305 NORTH MILITARY TRAIL WEST PALM BEACH FL, 33410-6400		Project Title REMOVE AND REPLACE PUBLIC ADDRESS SYSTEM Approved Date: DECEMBER 14, 2022 Checked: JDM Drawn: HT		VA PROJECT NUMBER 548-22-100 Building Number # Drawing Number T-122 Dwg 14 of 32	
		SEAL 52505 12/15/2022									
		REVISIONS:									

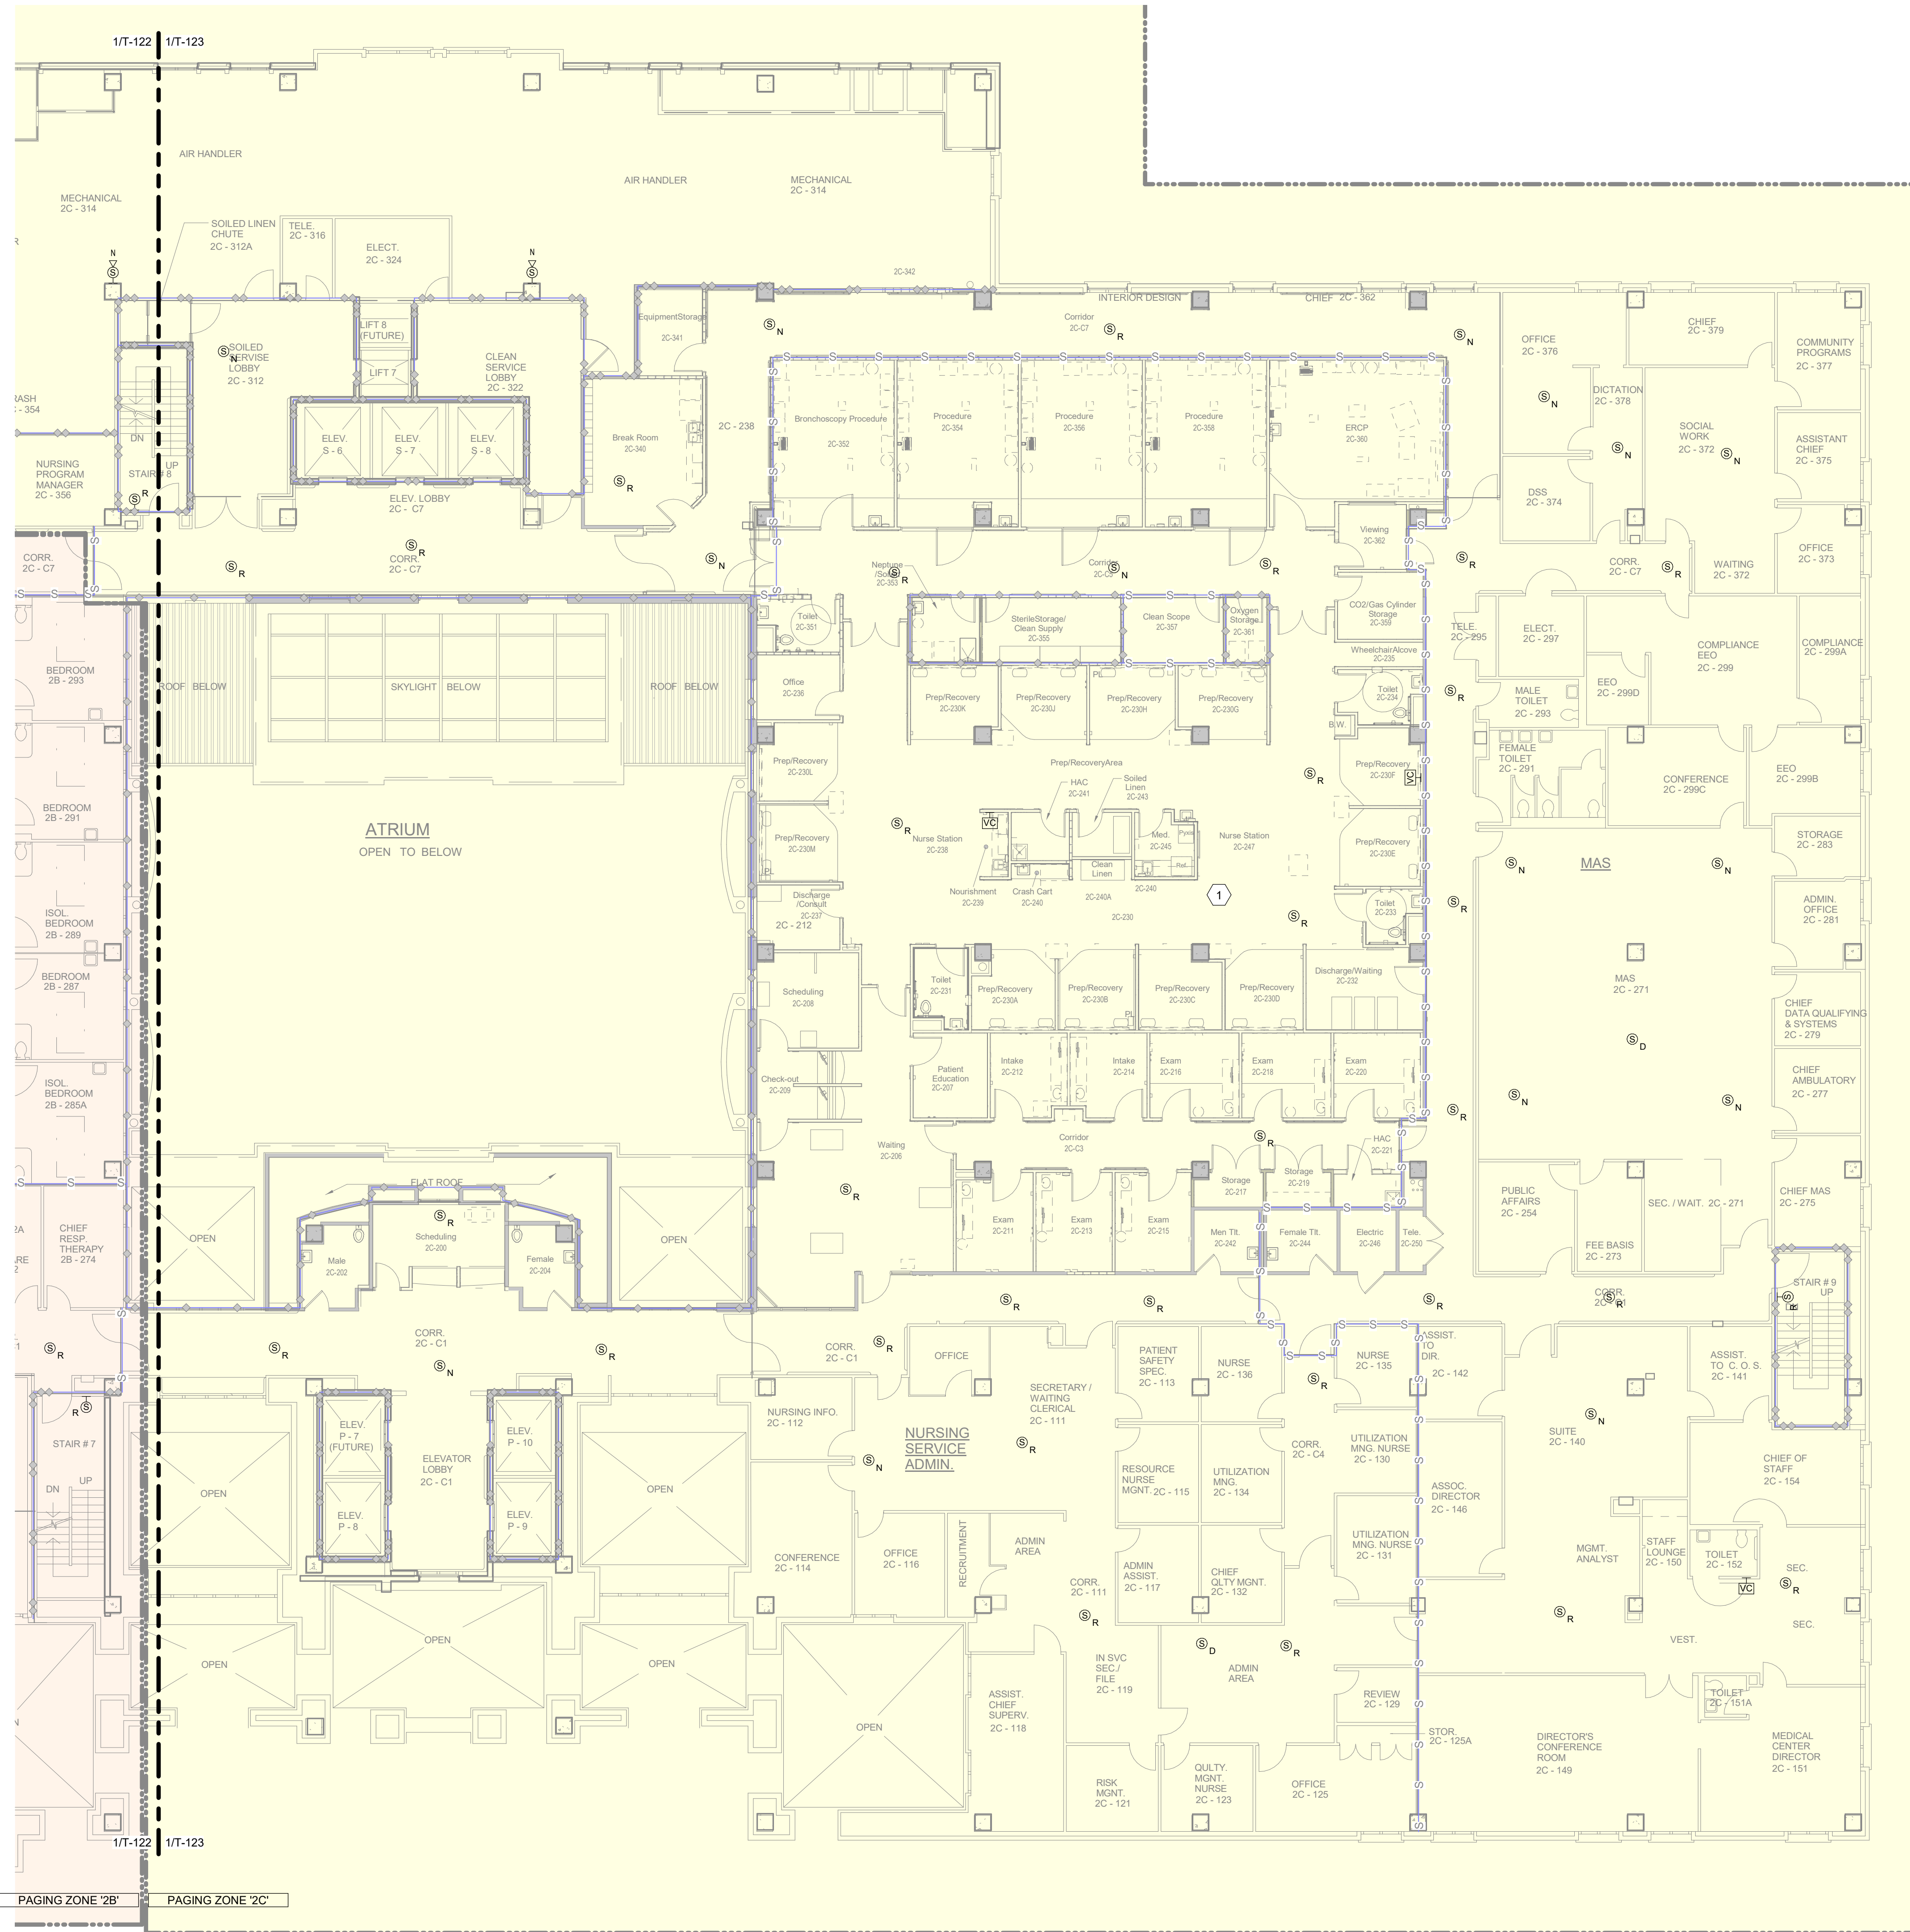

1 SECOND FLOOR NW PAMNS
Scale: 3/32" = 1'-0"

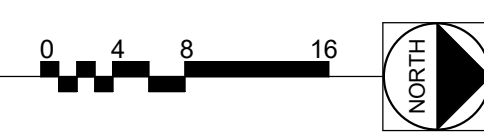


- SHEET NOTES:**
- A. PROVIDE PAMNS DEVICES AT LOCATIONS INDICATED ON PLANS. PROVIDE WIRING AND CIRCUIT AS INDICATED ON DETAILS.
 - B. ALL PAMN WIRING SHALL BE CONCEALED IN WALLS, IN RACEWAY OR AND ABOVE THE CEILING IN CONDUIT.
 - C. PAMN WIRING IN UNFINISHED AREAS SHALL BE IN SURFACE MOUNTED RACEWAY (MECH. ROOM, ROOMS WITH NO CEILINGS.)
 - D. ALL CEILING SPEAKERS SHALL BE SET AT 1/2 WATT UNLESS NOTED OTHERWISE.
 - E. ALL WALL MOUNTED SPEAKERS SHALL BE SET AT 4 WATTS UNLESS NOTED OTHERWISE.
 - F. CONTRACTOR RESPONSIBLE FOR PROVIDING AND INSTALLING FIRE SLEEVES FOR FIREWALL. CONTRACTOR SHALL ADEQUATELY REPAIR ANY FIREWALL PENETRATIONS.

- KEY NOTES:**
- 1 VOLUME CONTROL FOR PREP/RECOVERY AREA, WAITING 2C-208 AND CORRIDORS 2C-353, 2C-C5, AND 2C-2C-3.

ABBREVIATED SYMBOL LEGEND

SYMBOL	HEIGHT	DESCRIPTION
Ⓢ	CEILING	CEILING MOUNTED SPEAKER
Ⓢ	96"	WALL MOUNTED SPEAKER
Ⓢ	AS NOTED	WALL MOUNTED HORN
Ⓢ	48"	VOLUME CONTROL
Ⓢ	48"	PAGING CONSOLE
Ⓢ	FLOOR	PAGING CABINET

DEVICES WITH THE FOLLOWING TAGS ARE AS INDICATED:
E. EXISTING DEVICES TO REMAIN. PROVIDE NEW CABLING AND CONDUIT AS NEEDED.
D. EXISTING DEVICES TO BE DEMOLISHED BY THE CONTRACTOR.
R. EXISTING DEVICES TO BE REPLACED WITH NEW BY THE CONTRACTOR.
N. NEW DEVICES TO BE PROVIDED AND INSTALLED BY THE CONTRACTOR.
ALL HEIGHTS ARE TO CENTER OF DEVICE UNLESS NOTED OTHERWISE. HEIGHTS INDICATED IN PLANS SHALL SUPERSEDE THOSE LISTED HERE.

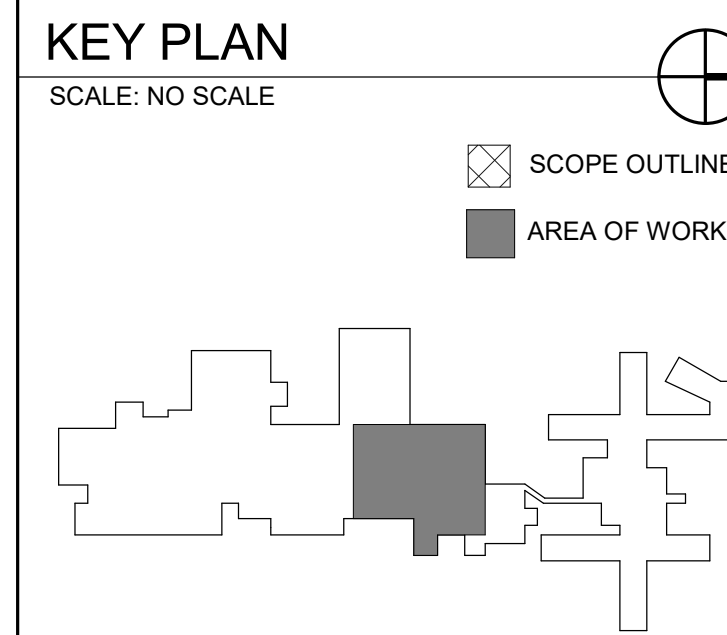


WALL RATING LEGEND

—•—•—•—	1 HR - FIRE SEPARATION
—•—•—•—	2 HR - FIRE SEPARATION
—•—•—•—	SMOKE RESISTIVE HAZARDOUS AREA

**FULLY SPRINKLERED
100% CONSTRUCTION DOCUMENTS**

--	--	

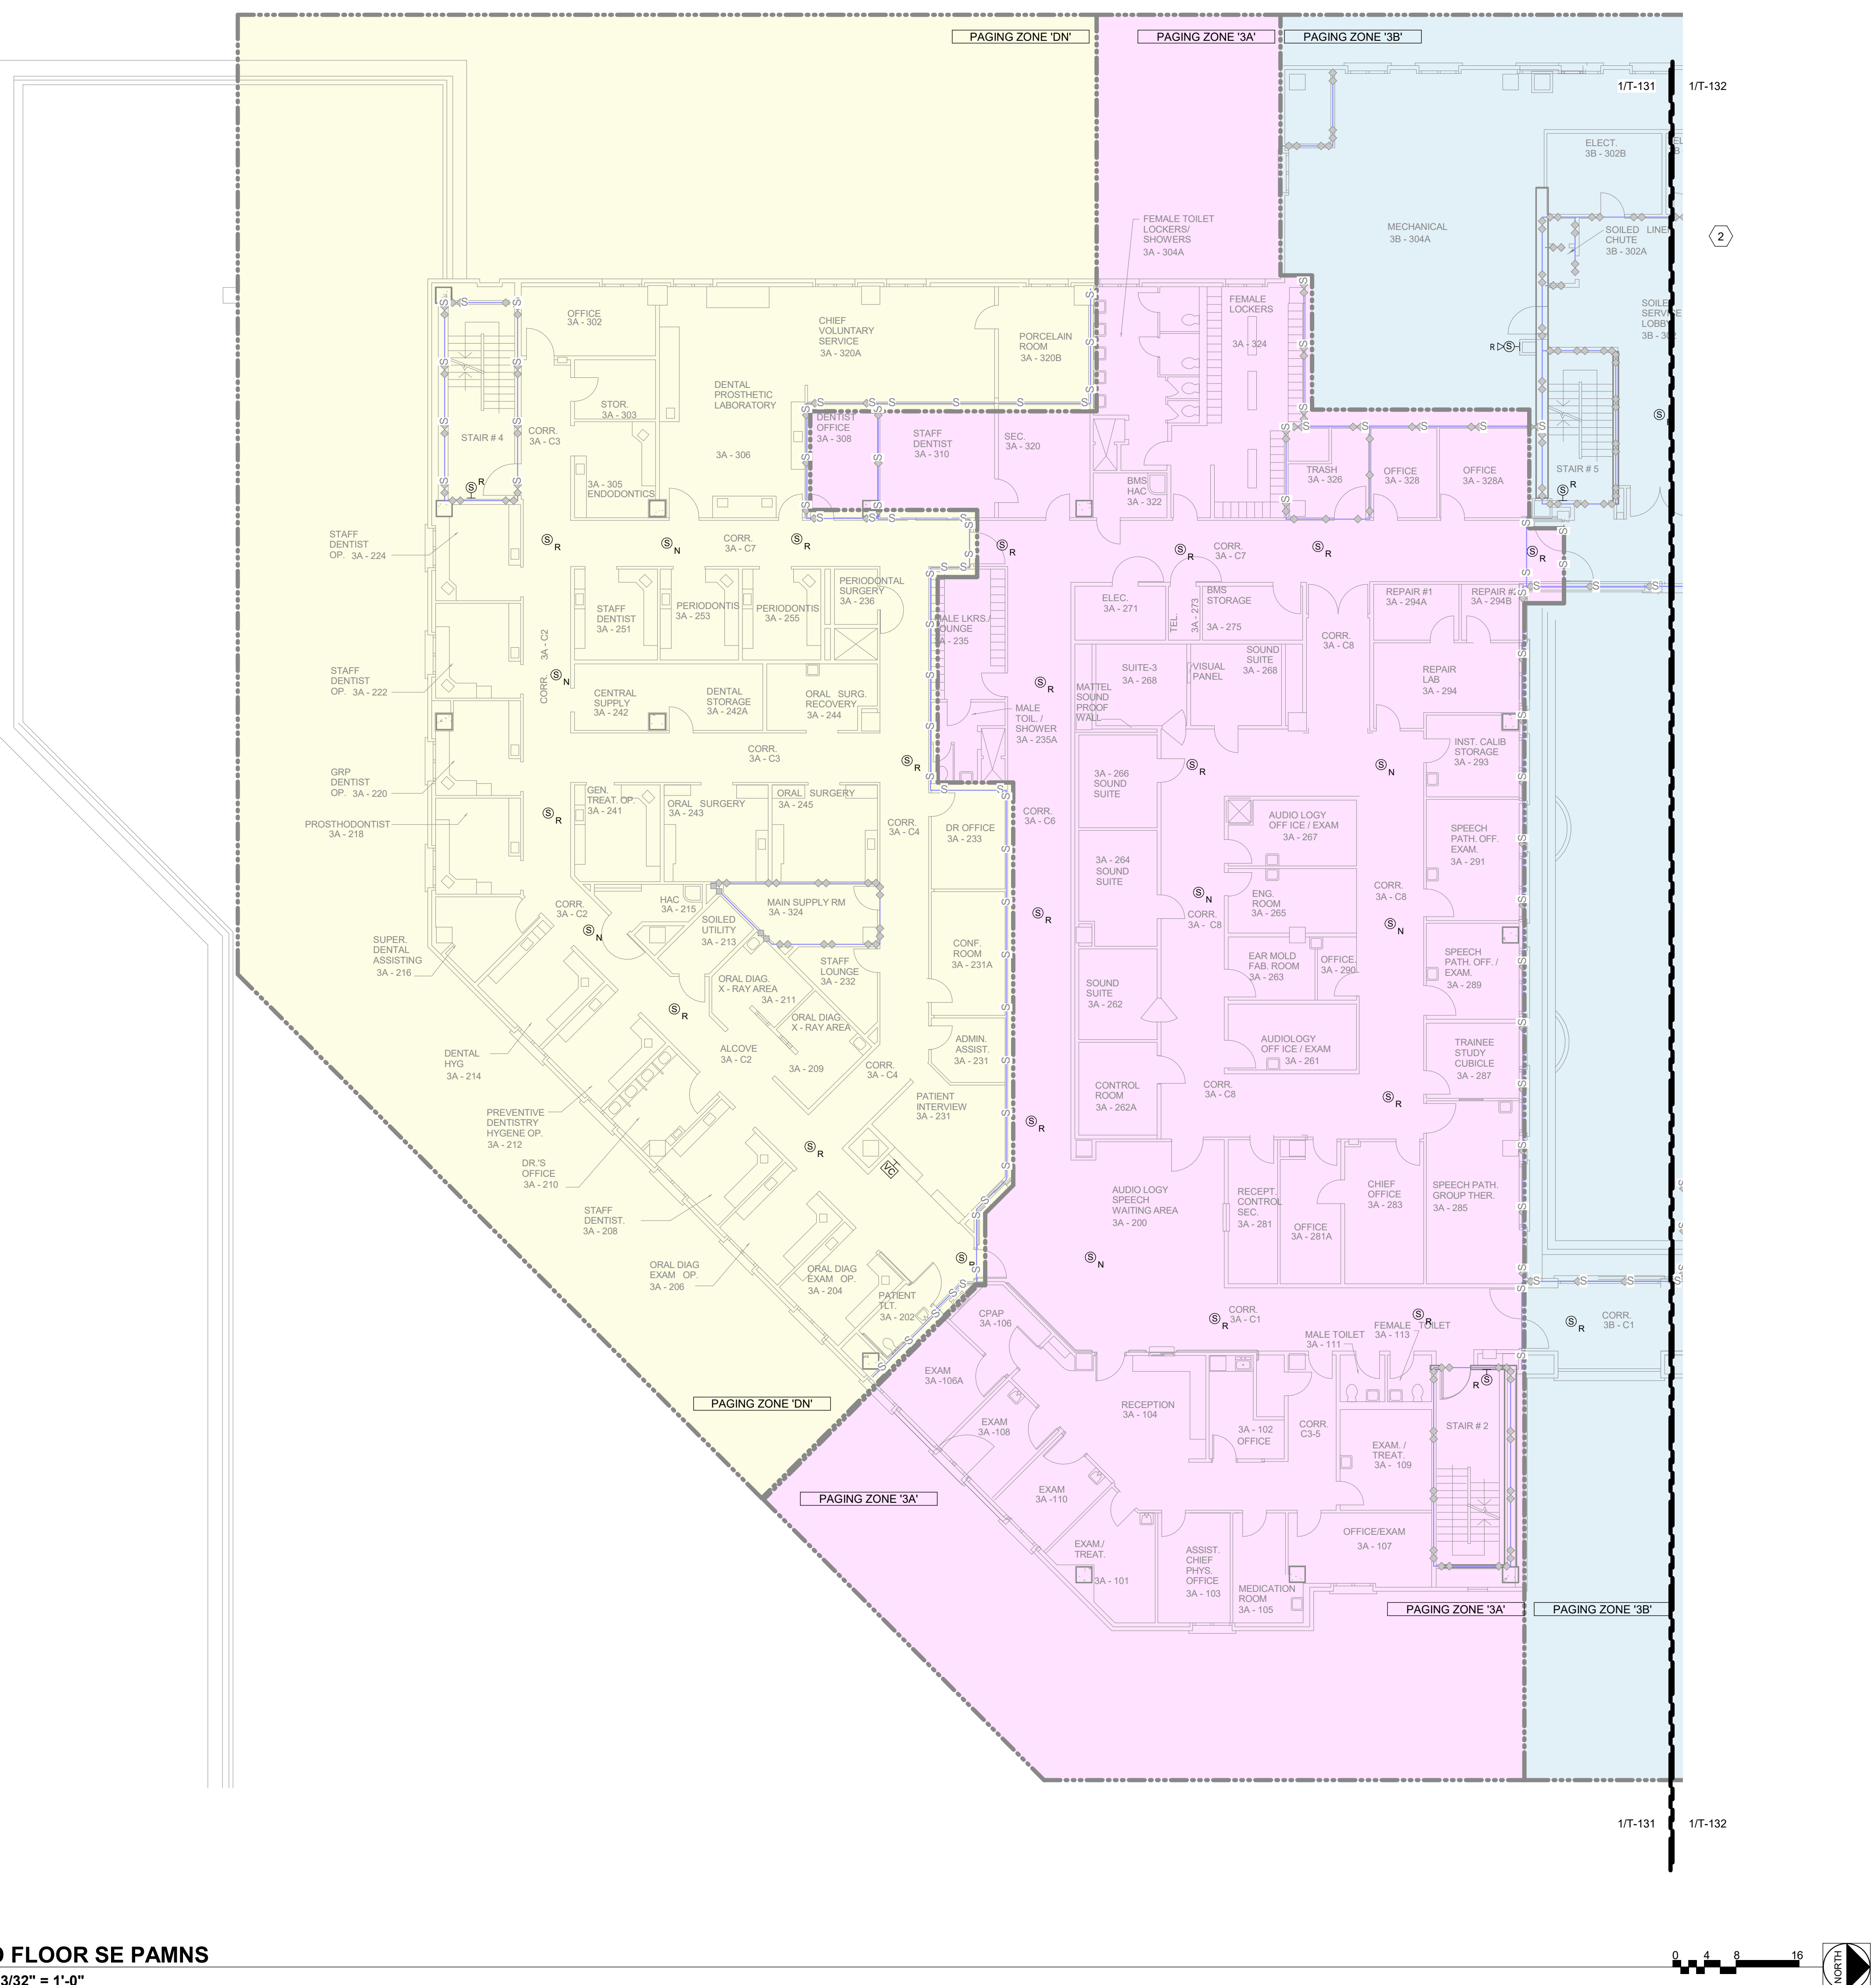

SHEET NOTES:

- A. PROVIDE PAINNS DEVICES AT LOCATIONS INDICATED ON PLANS. PROVIDE WIRING AND CIRCUIT AS INDICATED ON DETAILS.
- B. ALL PAMM WIRING SHALL BE CONCEALED IN WALLS, IN RACEWAY OR AND ABOVE THE CEILS IN CONDUIT.
- C. PAMM WIRING IN UNFINISHED AREAS SHALL BE IN SURFACE MOUNTED RACEWAY (MECH. ROOM, ROOMS WITH NO CEILINGS.)
- D. ALL CEILING SPEAKERS SHALL BE SET AT 1/2 WALL UNLESS NOTED OTHERWISE.
- E. ALL WALL MOUNTED SPEAKERS SHALL BE SET AT 4 WALLS UNLESS NOTED OTHERWISE.
- F. CONTRACTOR RESPONSIBLE FOR PROVIDING AND INSTALLING FIRE SLEEVES FOR FIREWALL. CONTRACTOR SHALL ADEQUATELY REPAIR ANY FIREWALL PENETRATIONS.

KEY NOTES:

**ABBREVIATED SYMBOL
LEGEND**

SYMBOL	HEIGHT	DESCRIPTION
	CEILING	CEILING MOUNTED SPEAKER
	96"	WALL MOUNTED SPEAKER
	AS NOTED	WALL MOUNTED HORN
	48"	VOLUME CONTROL
	48"	PAGING CONSOLE
	FLOOR	PAGING CABINET

DEVICES WITH THE FOLLOWING TAGS ARE AS INDICATED:

C: EXISTING DEVICES TO REMAIN. PROVIDE NEW CABLING AND CONDUIT AS NEEDED.

D: EXISTING DEVICES TO BE DEMOLISHED BY THE CONTRACTOR.



R: EXISTING DEVICES TO BE REPLACED WITH NEW BY THE CONTRACTOR.

N: NEW DEVICES TO BE PROVIDED AND INSTALLED BY THE CONTRACTOR.


ALL DEVICES ARE TO BE IDENTIFIED BY DEVICE UNLESS NOTED OTHERWISE. HEIGHTS INDICATED IN PLANS SHALL SUPERSEDE THOSE LISTED HERE.

KEY PLAN

SCALE: NO SCALE

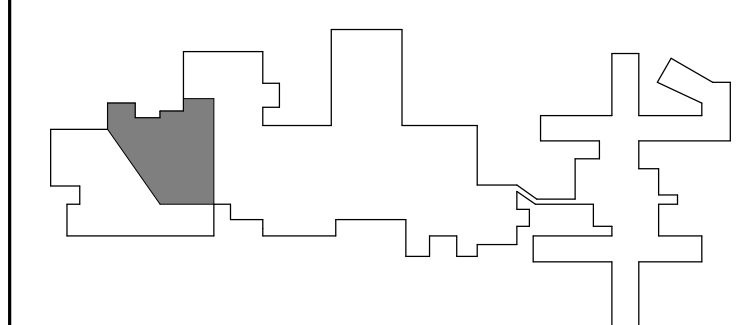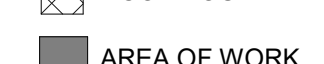


WALL RATING LEGEND

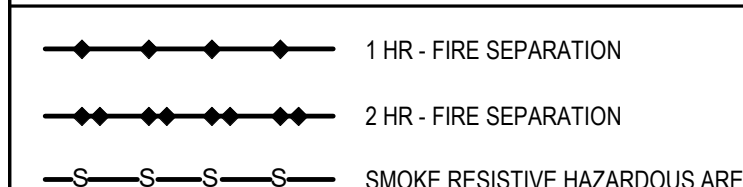


FULLY SPRINKLERED
100% CONSTRUCTION DOCUMENTS

--	--	

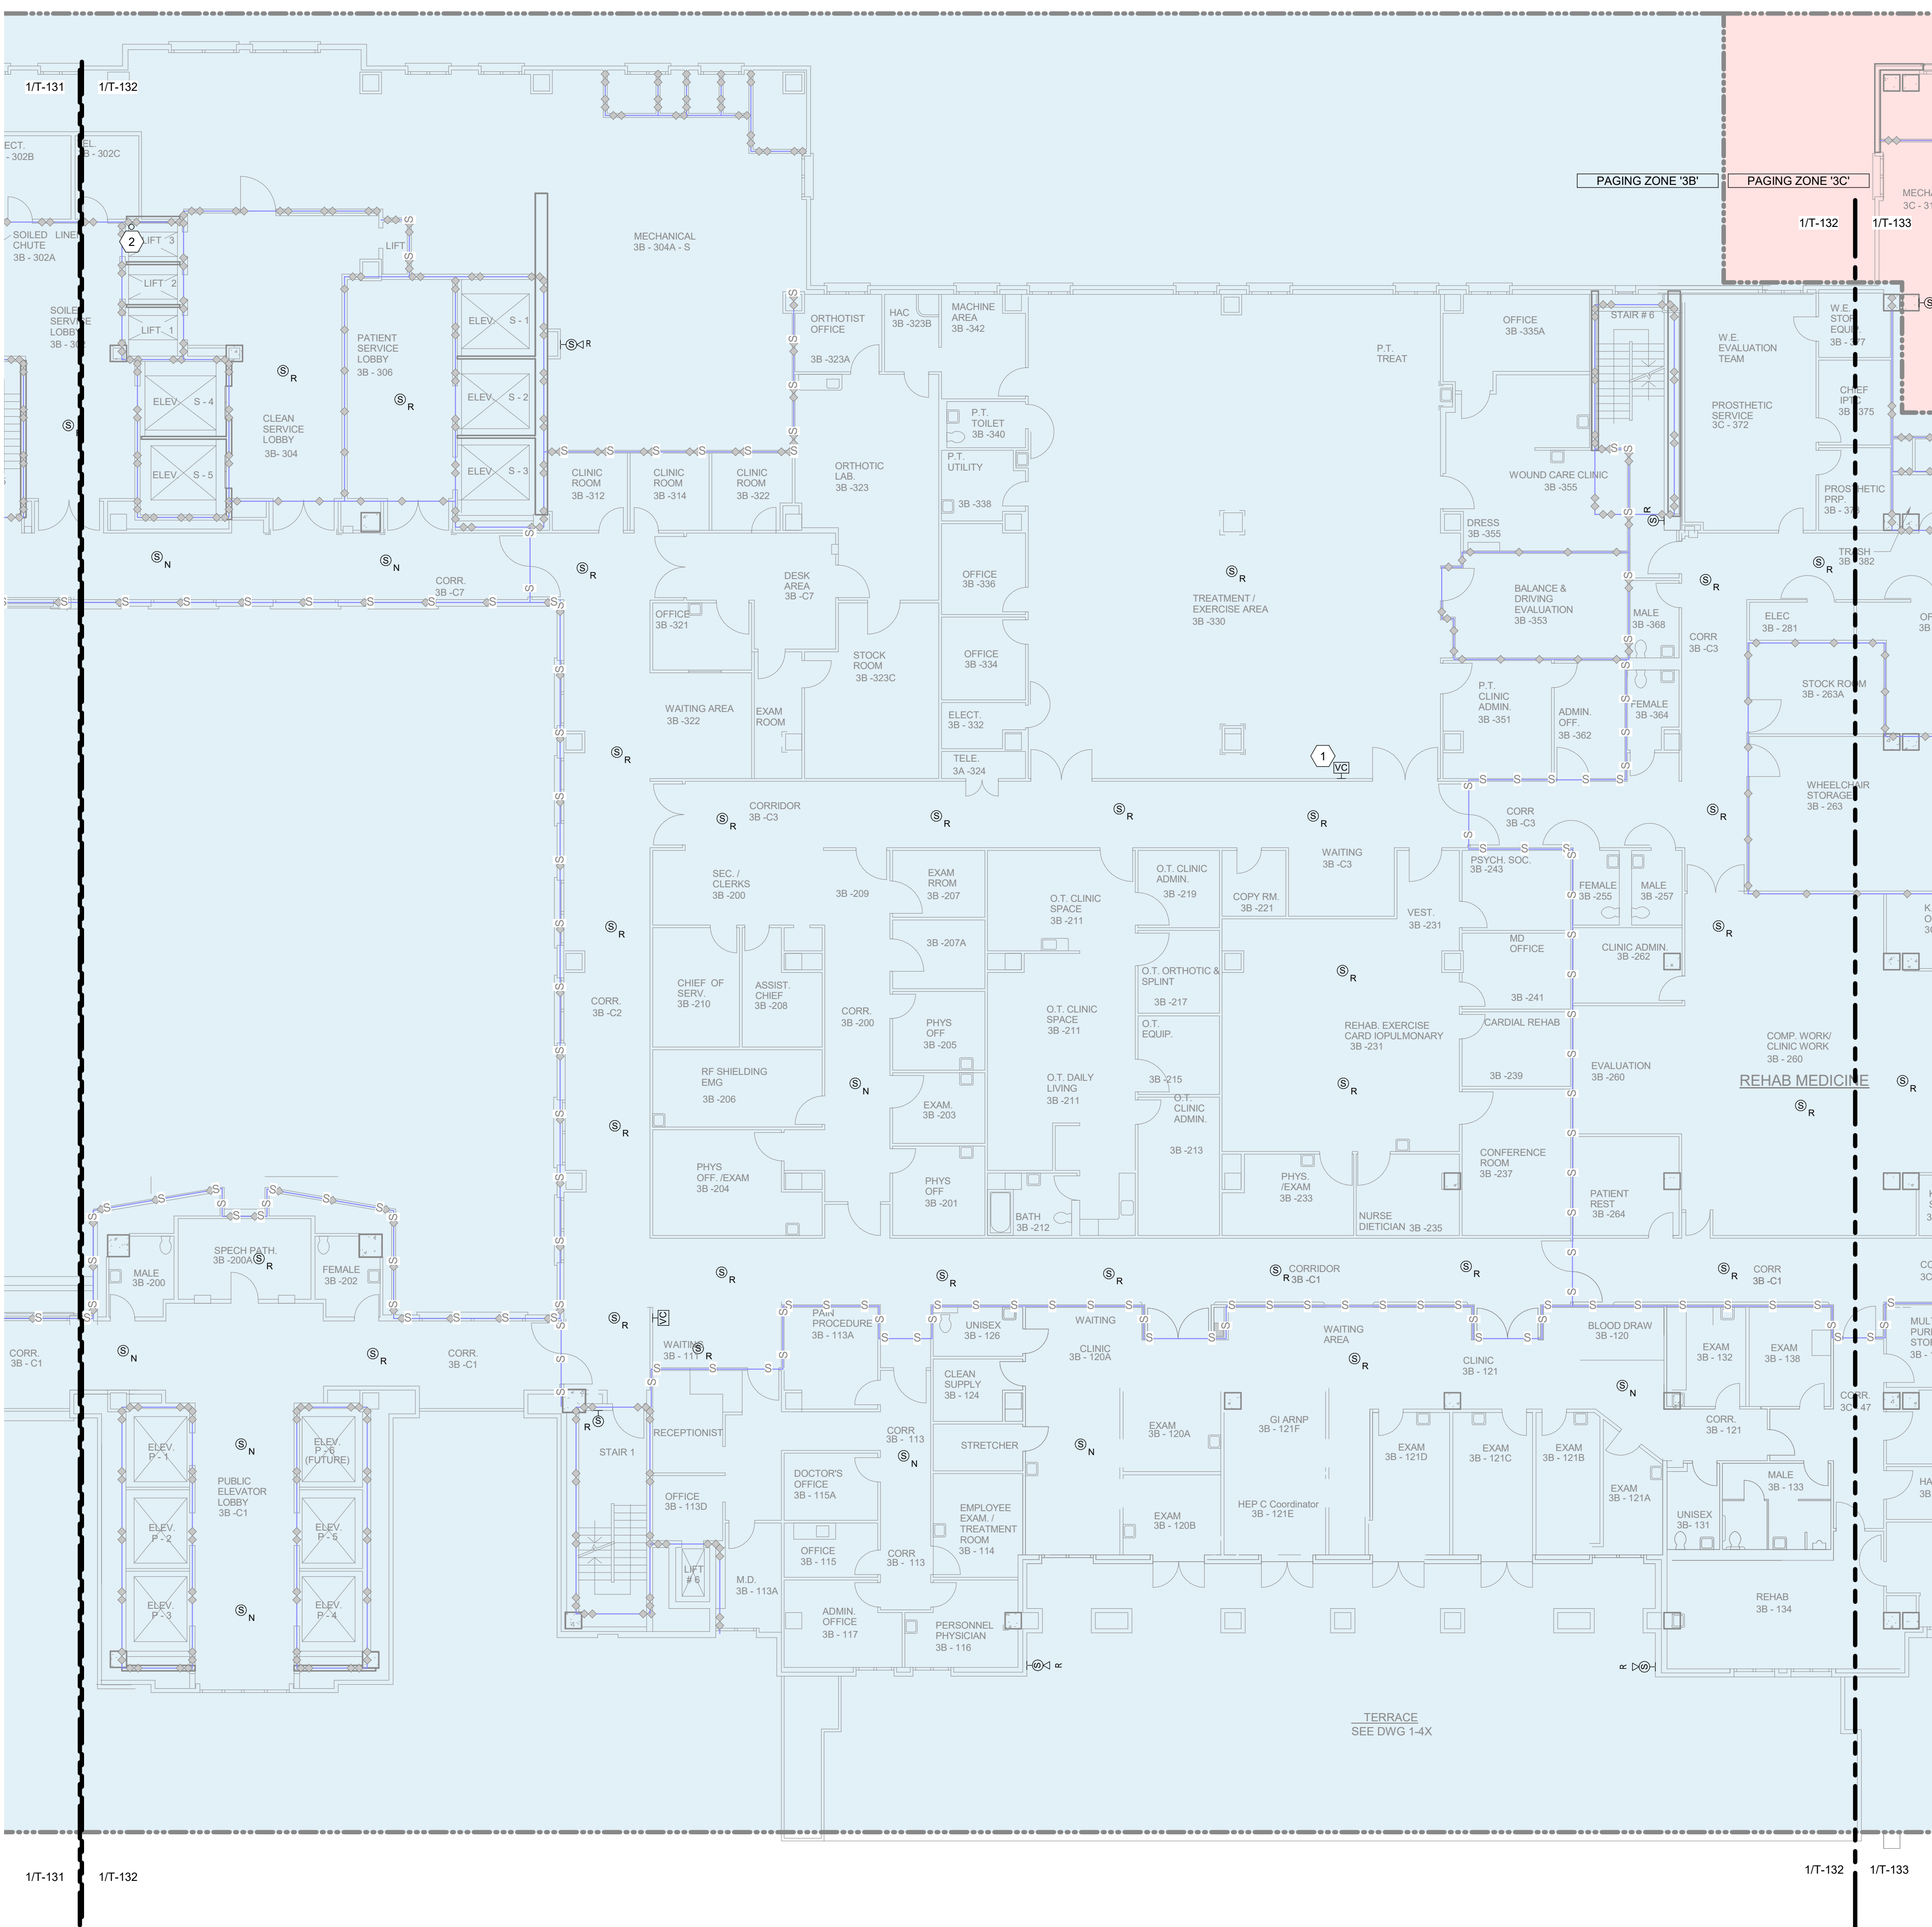

1 THIRD FLOOR CENT PAMNS
Scale: 3/32" = 1'-0"

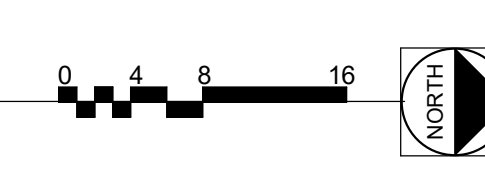

SHEET NOTES:

- A. PROVIDE PAMNS DEVICES AT LOCATIONS INDICATED ON PLANS. PROVIDE WIRING AND CIRCUIT AS INDICATED ON DETAILS.
- B. ALL PAMN WIRING SHALL BE CONCEALED IN WALLS, IN RACEWAY OR AND ABOVE THE CEILING IN CONDUIT.
- C. PAMN WIRING IN UNFINISHED AREAS SHALL BE IN SURFACE MOUNTED RACEWAY (MECH. ROOM, ROOMS WITH NO CEILINGS.)
- D. ALL CEILING SPEAKERS SHALL BE SET AT 1/2 WATT UNLESS NOTED OTHERWISE.
- E. ALL WALL MOUNTED SPEAKERS SHALL BE SET AT 4 WATTS UNLESS NOTED OTHERWISE.
- F. CONTRACTOR RESPONSIBLE FOR PROVIDING AND INSTALLING FIRE SLEEVES FOR FIREWALL. CONTRACTOR SHALL ADEQUATELY REPAIR ANY FIREWALL PENETRATIONS.

KEY NOTES:

- 1 VOLUME CONTROL FOR TREATMENT EXERCISE AREA 3B-330.
- 2 LOCATION OF VERTICAL RISER IN LIFT SHAFT. REF. T-601.

ABBREVIATED SYMBOL LEGEND

SYMBOL	HEIGHT	DESCRIPTION
Ⓢ	CEILING	CEILING MOUNTED SPEAKER
Ⓢ	96"	WALL MOUNTED SPEAKER
Ⓢ	AS NOTED	WALL MOUNTED HORN
Ⓢ	48"	VOLUME CONTROL
Ⓢ	48"	PAGING CONSOLE
Ⓢ	FLOOR	PAGING CABINET

DEVICES WITH THE FOLLOWING TAGS ARE AS INDICATED:
E: EXISTING DEVICES TO REMAIN. PROVIDE NEW CABLING AND CONDUIT AS NEEDED.
D: EXISTING DEVICES TO BE DEMOLISHED BY THE CONTRACTOR.
R: EXISTING DEVICES TO BE REPLACED WITH NEW BY THE CONTRACTOR.
N: NEW DEVICES TO BE PROVIDED AND INSTALLED BY THE CONTRACTOR.
ALL HEIGHTS ARE TO CENTER OF DEVICE UNLESS NOTED OTHERWISE. HEIGHTS INDICATED IN PLANS SHALL SUPERSEDE THOSE LISTED HERE.

KEY PLAN


SCALE: NO SCALE


SCOPE OUTLINE
AREA OF WORK

WALL RATING LEGEND

—•—•—•—	1 HR - FIRE SEPARATION
—•—•—•—	2 HR - FIRE SEPARATION
—•—•—•—	SMOKE RESISTIVE HAZARDOUS AREA

FULLY SPRINKLERED
100% CONSTRUCTION DOCUMENTS
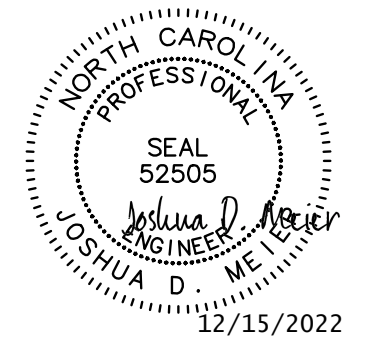
#	Revisions:	Date	CONSULTANTS:	 DESIGNED BY Bicsi Glenn D. Althrock III BICS ID # 363972 EXPIRES 12-31-24 RCDD 12/15/2022	 SEAL 52505 12/15/2022 JOSHUA D. WILSON P.E. 12/15/2022	PROJECT MANAGER Headquarters: Apogee Consulting Group, P.A. 1151 Kildaire Farm Road, Suite 120 Cary, North Carolina 27511 www.acg-pa.com 919-858-7420		Office of Construction and Facilities Management VA U.S. Department of Veterans Affairs	Drawing Title THIRD FLOOR CENT PAMNS		Project Title REMOVE AND REPLACE PUBLIC ADDRESS SYSTEM		VA PROJECT NUMBER 548-22-100	
						Location WEST PALM BEACH VAMC 7305 NORTH MILITARY TRAIL WEST PALM BEACH FL, 33410-6400			Approved		Building Number #			
						Date DECEMBER 14, 2022			Checked JDM		Drawing Number T-132			
									Drawn HT		Dwg 17 of 32			

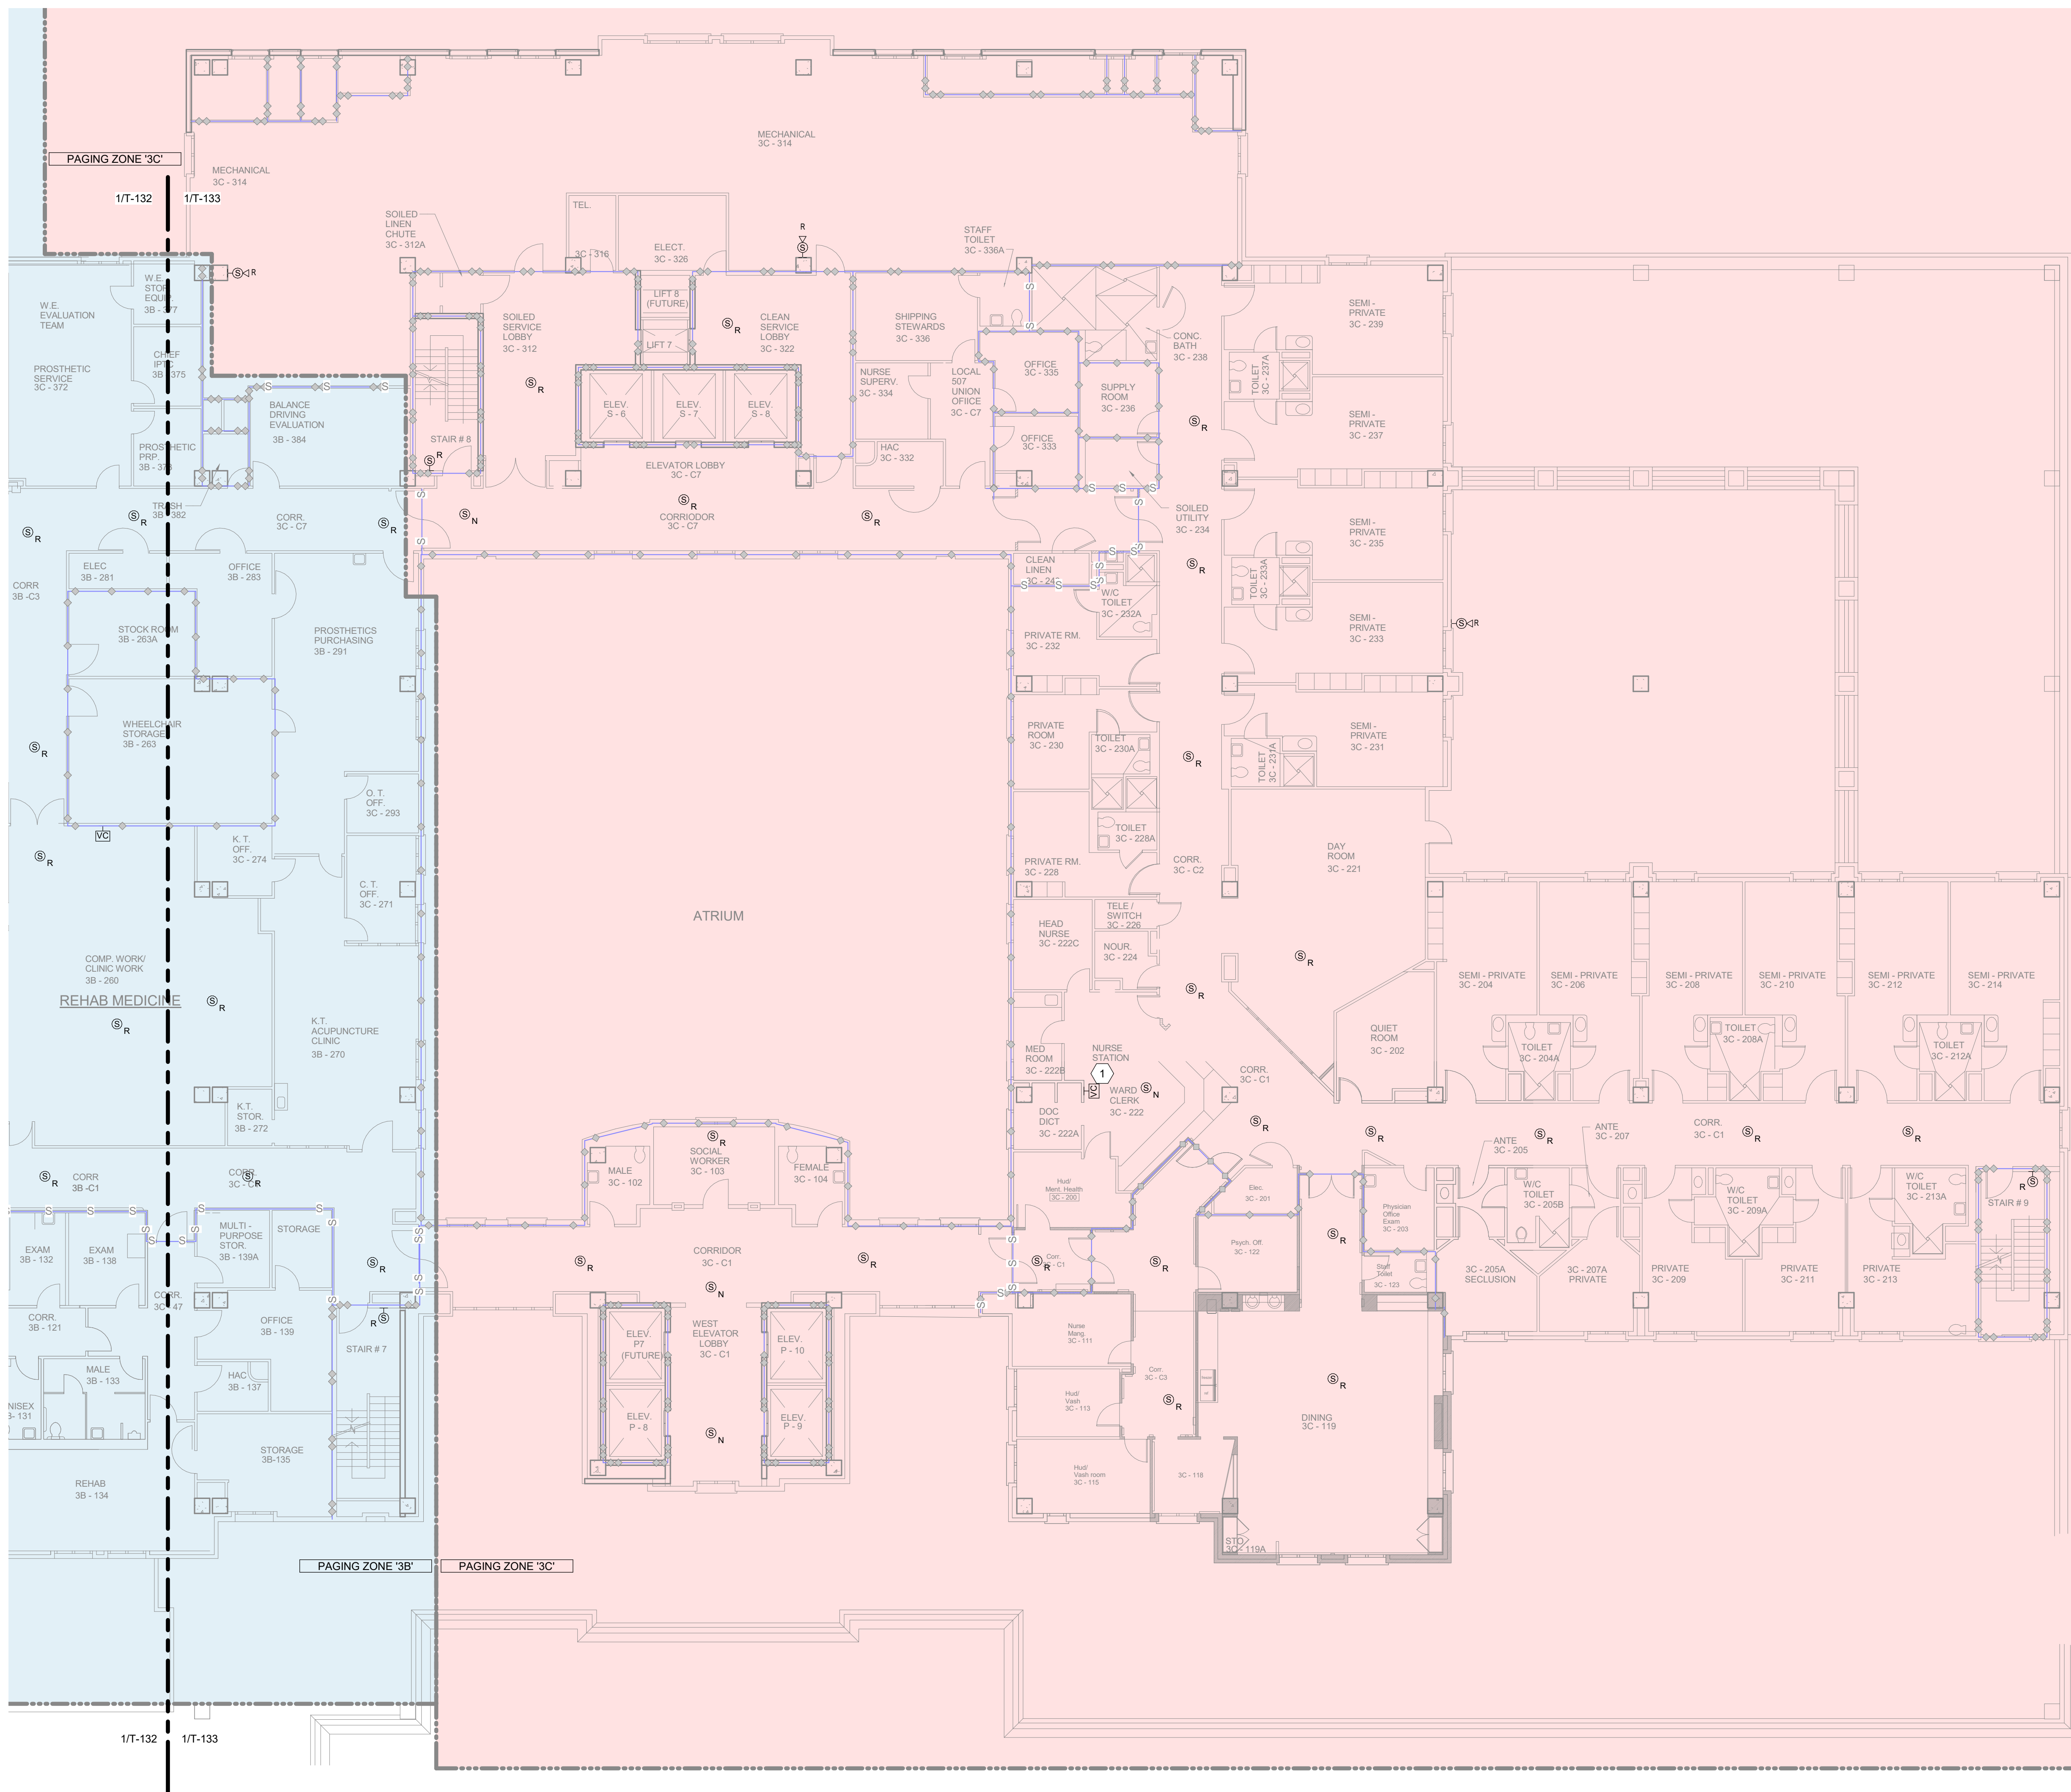

SHEET NOTES:

- A. PROVIDE PAMNS DEVICES AT LOCATIONS INDICATED ON PLANS. PROVIDE WIRING AND CIRCUIT AS INDICATED ON DETAILS.
- B. ALL PAMM WIRING SHALL BE CONCEALED IN WALLS, IN RACEWAY OR AND ABOVE THE CEILING IN CONDUIT.
- C. PAMM WIRING IN UNFINISHED AREAS SHALL BE IN SURFACE MOUNTED RACEWAY (MECH. ROOM, ROOMS WITH NO CEILINGS.)
- D. ALL CEILING SPEAKERS SHALL BE SET AT 1/2 WATT UNLESS NOTED OTHERWISE.
- E. ALL WALL MOUNTED SPEAKERS SHALL BE SET AT 4 WATTS UNLESS NOTED OTHERWISE.
- F. CONTRACTOR RESPONSIBLE FOR PROVIDING AND INSTALLING FIRE SLEEVES FOR FIREWALL. CONTRACTOR SHALL ADEQUATELY REPAIR ANY FIREWALL PENETRATIONS.
- G. SPEAKERS IN 3P SHAL BE ANTILIGATURE AND UTILIZE TAMPER PROOF SECURITY SCREWS.

 KEY NOTES:

- 1 VOLUME CONTROL FOR DAY ROOM 3C-221,
DINING 3C-119 & CORRIDORS 3C-C1, 3C-C2,
3C-C3.

**ABBREVIATED SYMBOL
LEGEND**

SYMBOL	HEIGHT	DESCRIPTION
	CEILING	CEILING MOUNTED SPEAKER
	96"	WALL MOUNTED SPEAKER
	AS NOTED	WALL MOUNTED HORN
	48"	VOLUME CONTROL
	48"	PAGING CONSOLE
	FLOOR	PAGING CABINET

DEVICES WITH THE FOLLOWING TAGS ARE AS INDICATED:

INDICATED:
E: EXISTING DEVICES TO REMAIN. PROVIDE NEW

CABLING AND CONDUIT AS NEEDED.
D: EXISTING DEVICES TO BE DEMOLISHED BY

R: EXISTING DEVICES TO BE REPLACED WITH

N: NEW DEVICES TO BE PROVIDED AND

N: NEW DEVICES TO BE PROVIDED AND
INSTALLED BY THE CONTRACTOR.
ALL HEIGHTS ARE TO CENTER OF DEVICE UNLESS


ALL HEIGHTS ARE TO CENTER OF DEVICE UNLESS NOTED OTHERWISE. HEIGHTS INDICATED IN PLANS

SHALL SUPERSEDE THOSE LISTED HERE.


KEY PLAN

KEY PLAN

SCALE: NO SCALE

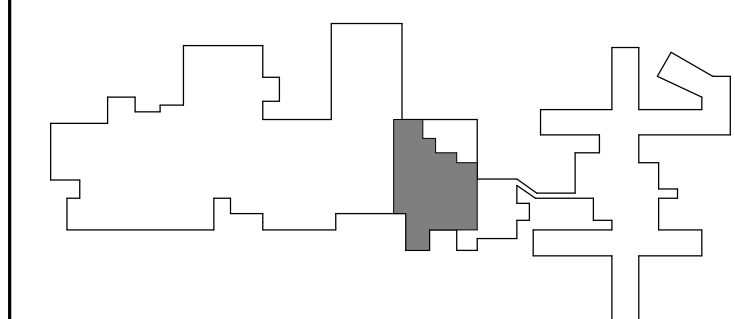

WALL RATING LEGEND

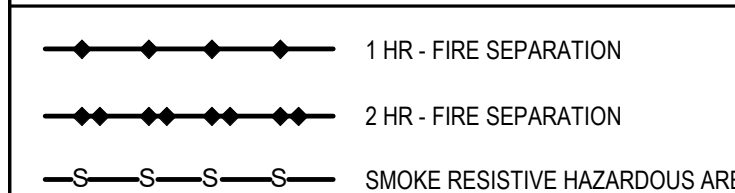

FULLY SPRINKLERED

100% CONSTRUCTION DOCUMENTS

	</
--	--	----

1

FOURTH FLOOR SE PAMNS
Scale: 3/32" = 1'-0"

CONSULTANTS:

Bicsi
Glenn D. Althoff III
BICS ID # 363972
EXPIRES 12-31-24
REGISTERED COMMUNICATIONS DESIGNER
RCDD 12/15/2022

PROFESSIONAL SEAL
Glenn D. Althoff III
BICS ID # 363972
EXPIRES 12-31-24
REGISTERED COMMUNICATIONS DESIGNER
RCDD 12/15/2022

PROJECT MANAGER
ACG Project Number 22-038
Headquarters:
Apogee Consulting Group, P.A.
1151 Kildaire Farm Road, Suite 120
Cary, North Carolina 27511
www.acg-pa.com 919-858-7420
© COPYRIGHT Apogee Consulting Group, P.A.


Office of Construction and Facilities Management
U.S. Department of Veterans Affairs

Drawing Title
FOURTH FLOOR SE PAMNS
Location
WEST PALM BEACH VAMC
7305 NORTH MILITARY TRAIL
WEST PALM BEACH FL, 33410-6400


Project Title
REMOVE AND REPLACE PUBLIC ADDRESS SYSTEM
Approved
Date DECEMBER 14, 2022
Checked JDM
Drawn HT

VA PROJECT NUMBER
548-22-100
Building Number

Drawing Number
T-141
Dwg 19 of 32

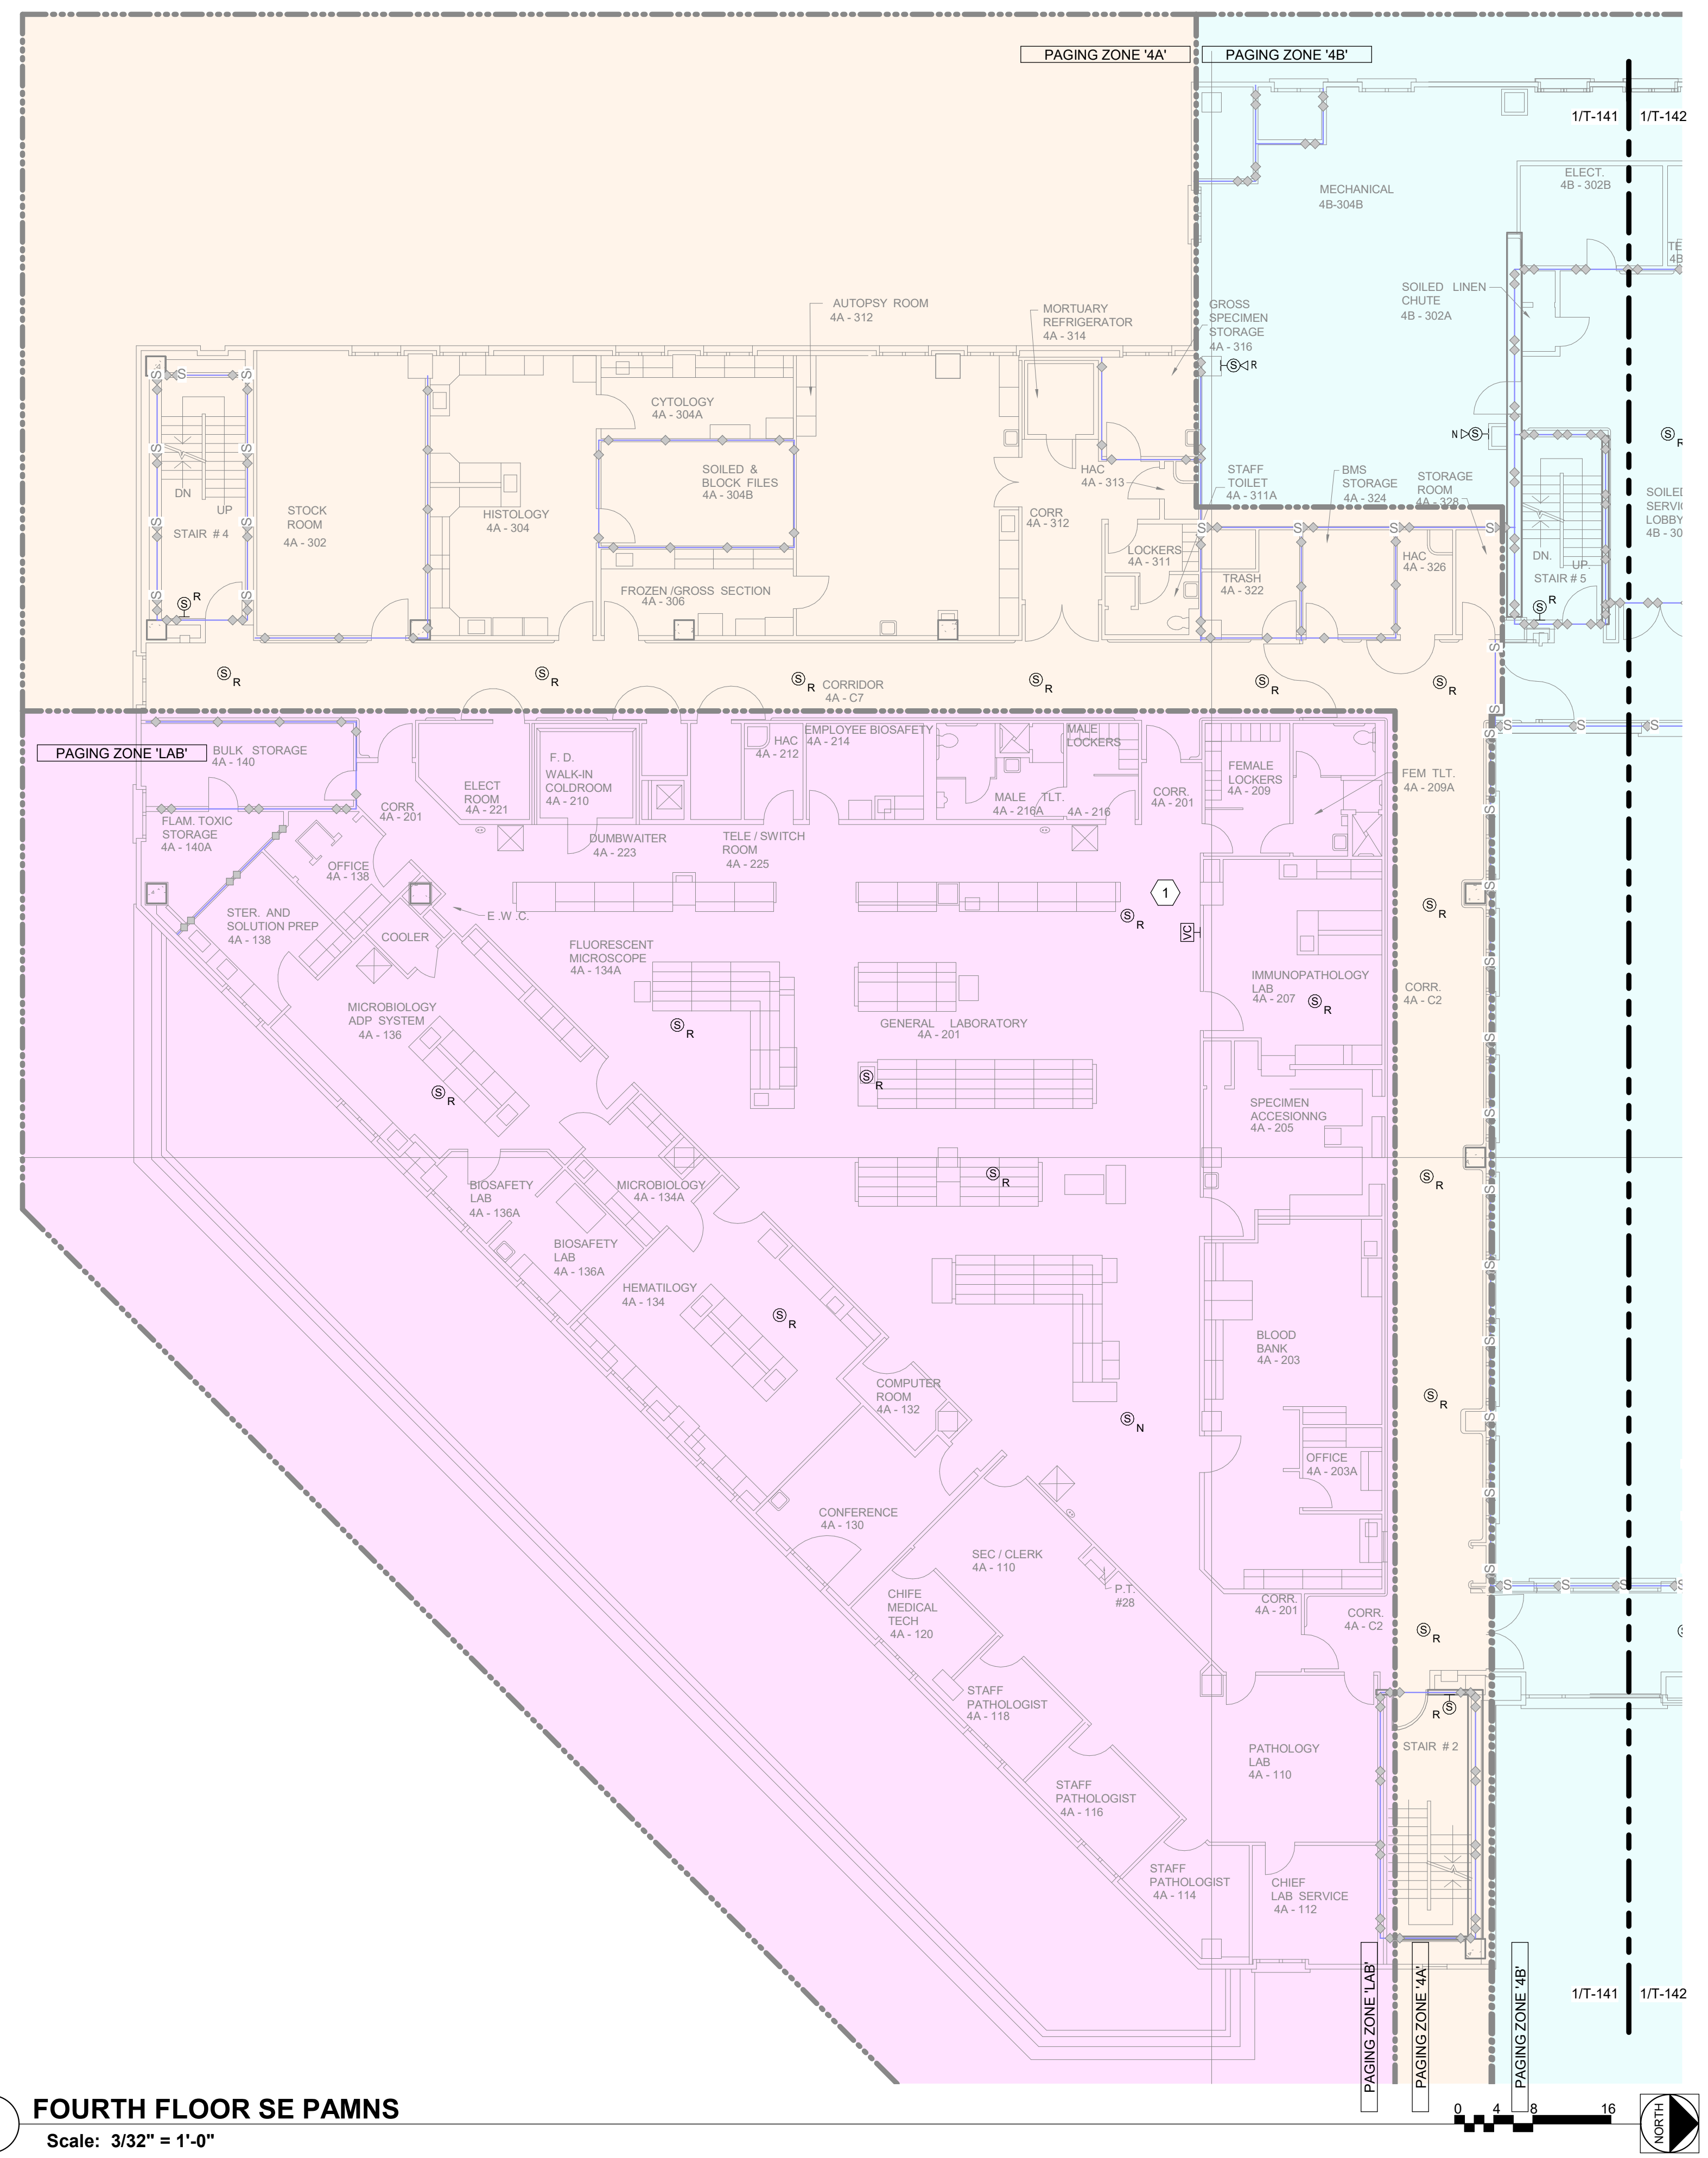

0	Project Title			VA PROJECT NUMBER
	REMOVE AND REPLACE PUBLIC ADDRESS SYSTEM			548-22-100
				Building Number
	Approved			#
	Date			Drawing Number
	DECEMBER 14, 2022	Checked JDM	Drawn HT	T-142
				Dwg 20 of 32

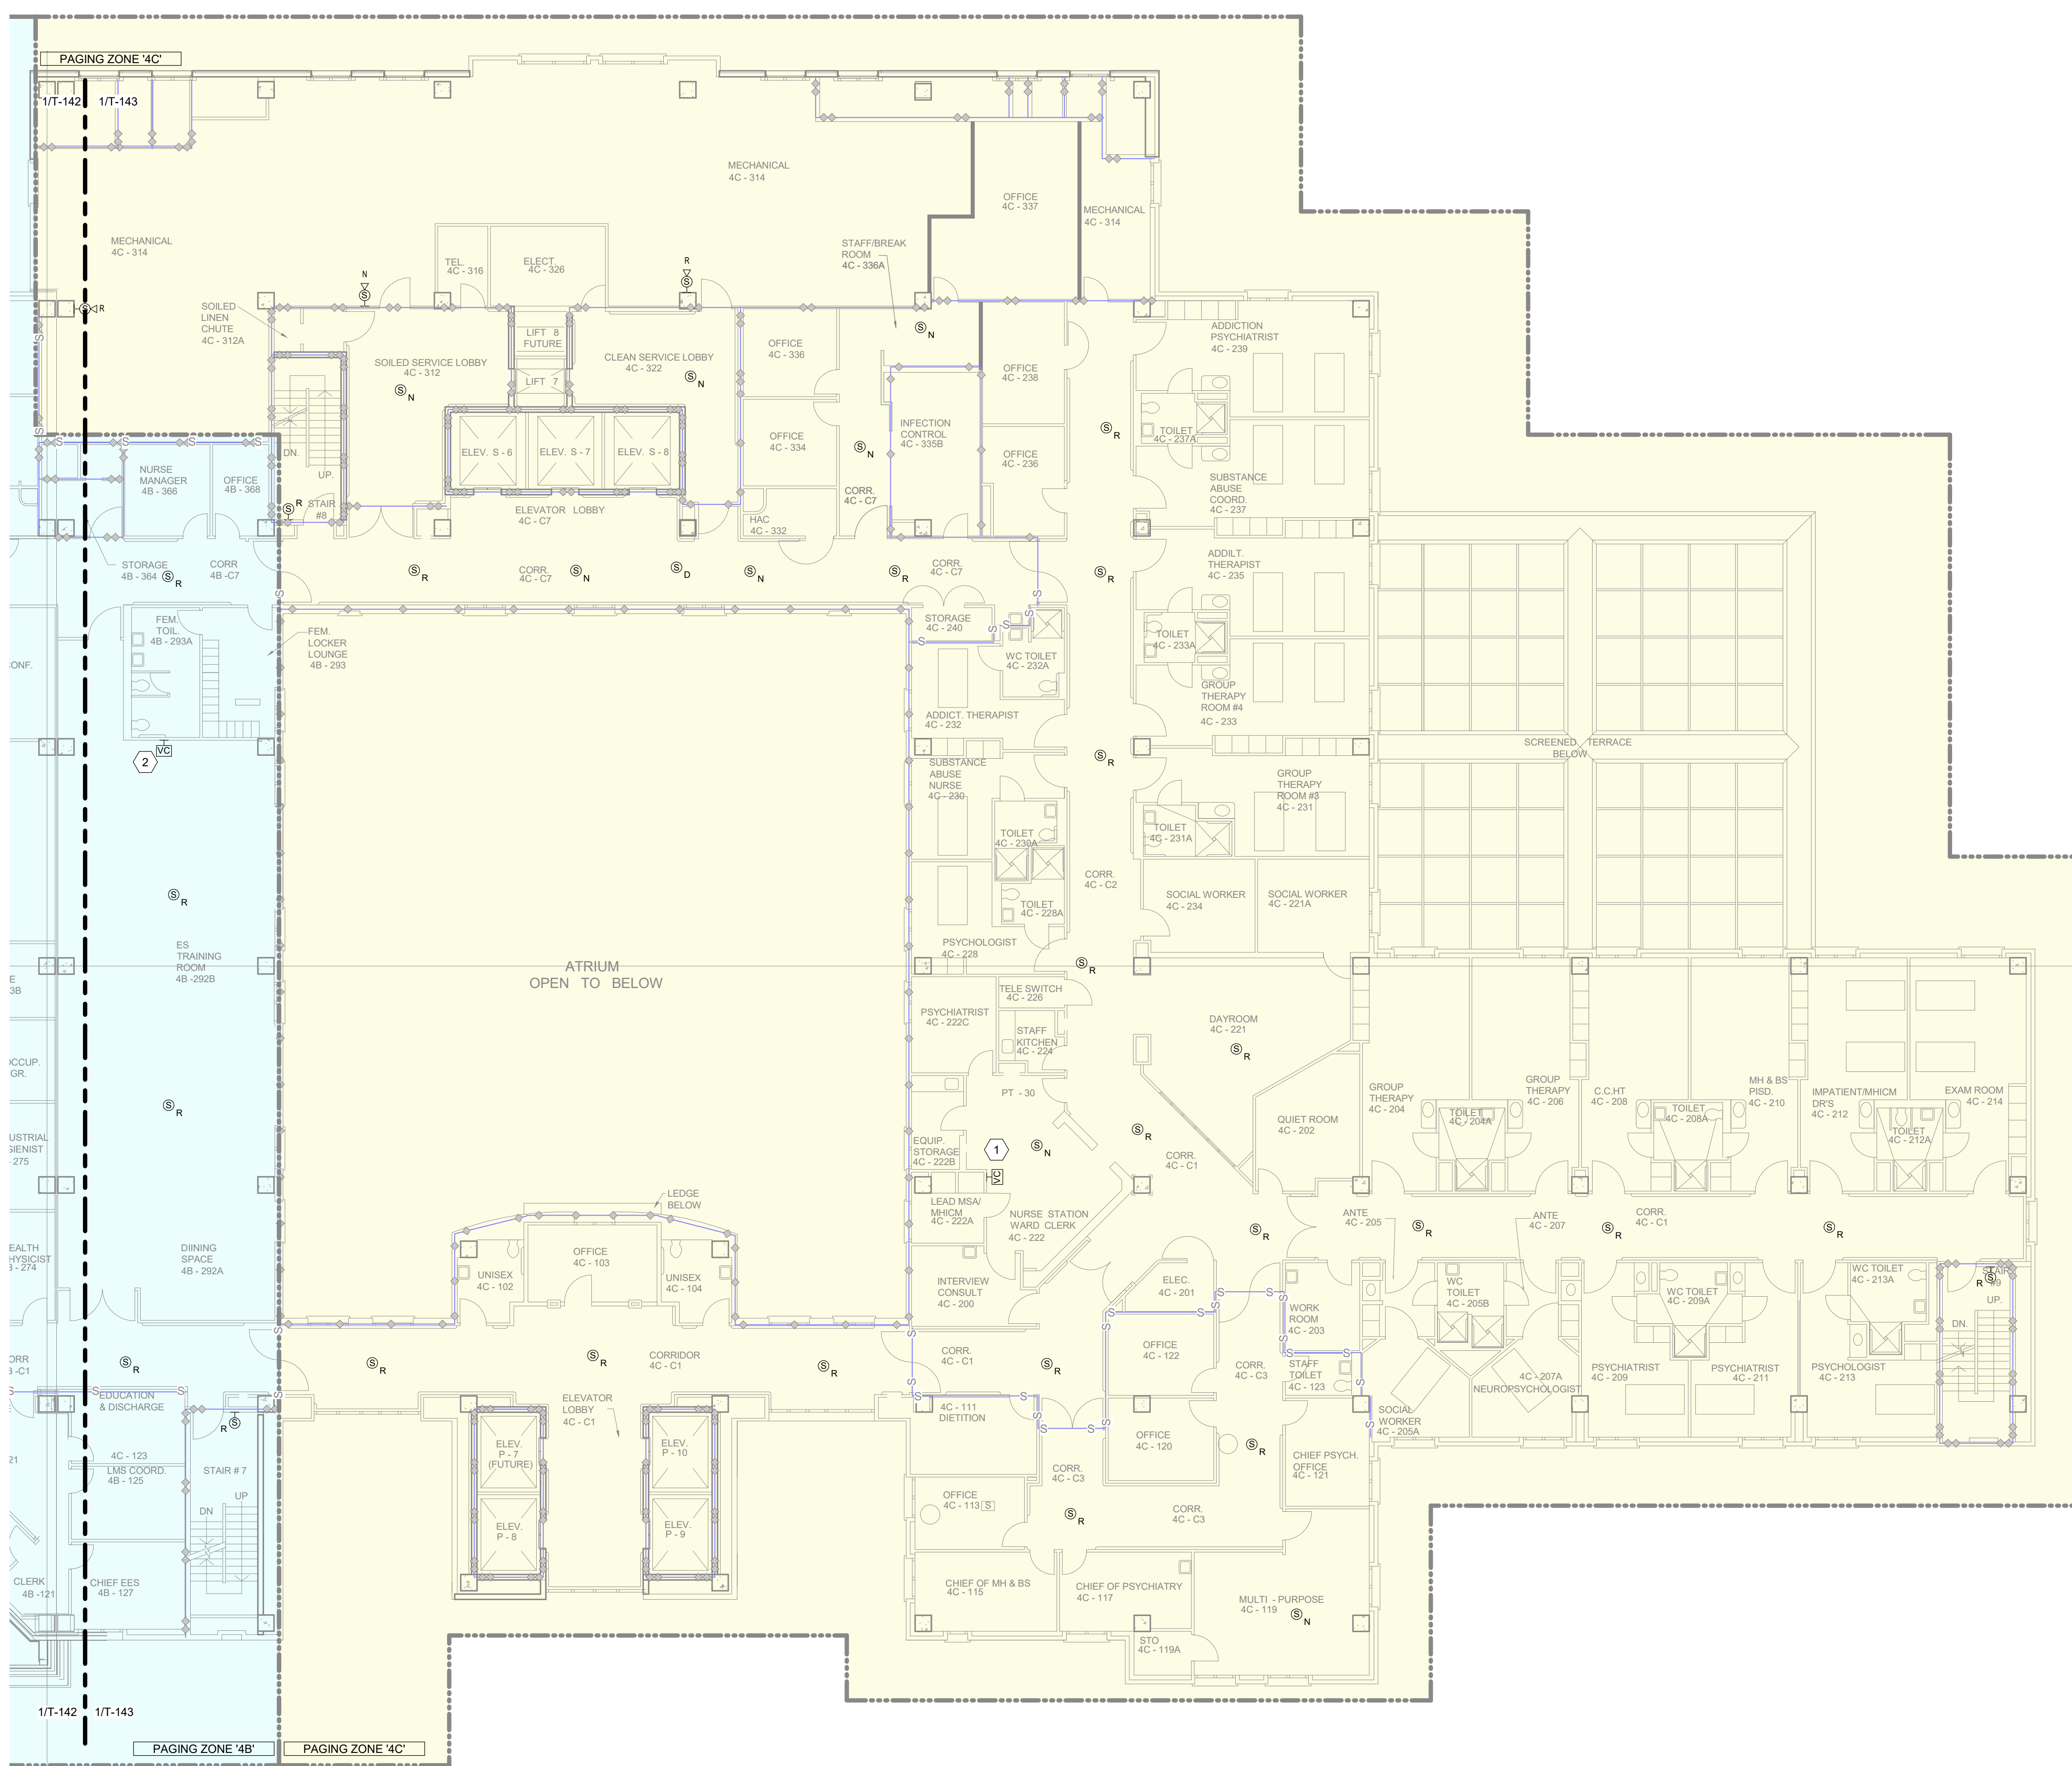

1 FOURTH FLOOR NW PAMNS
Scale: 3/32" = 1'-0"

SHEET NOTES:

- A. PROVIDE PAMNS DEVICES AT LOCATIONS INDICATED ON PLANS. PROVIDE WIRING AND CIRCUIT AS INDICATED ON DETAILS.
- B. ALL PAMN WIRING SHALL BE CONCEALED IN WALLS, IN RACEWAY OR AND ABOVE THE CEILING IN CONDUIT.
- C. PAMN WIRING IN UNFINISHED AREAS SHALL BE IN SURFACE MOUNTED RACEWAY (MECH. ROOM, ROOMS WITH NO CEILINGS.)
- D. ALL CEILING SPEAKERS SHALL BE SET AT 1/2 WATT UNLESS NOTED OTHERWISE.
- E. ALL WALL MOUNTED SPEAKERS SHALL BE SET AT 4 WATTS UNLESS NOTED OTHERWISE.
- F. CONTRACTOR RESPONSIBLE FOR PROVIDING AND INSTALLING FIRE SLEEVES FOR FIREWALL. CONTRACTOR SHALL ADEQUATELY REPAIR ANY FIREWALL PENETRATIONS.

KEY NOTES:

- 1 VOLUME CONTROL FOR NURSE STATION 4C-222, DAYROOM 4C-221 & CORRIDORS 4C-C1, 4C-C2, 4C-C3.

ABBREVIATED SYMBOL LEGEND

SYMBOL	HEIGHT	DESCRIPTION
Ⓢ	CEILING	CEILING MOUNTED SPEAKER
Ⓢ	96"	WALL MOUNTED SPEAKER
Ⓢ	AS NOTED	WALL MOUNTED HORN
Ⓢ	48"	VOLUME CONTROL
Ⓢ	48"	PAGING CONSOLE
Ⓢ	FLOOR	PAGING CABINET

DEVICES WITH THE FOLLOWING TAGS ARE AS INDICATED:
E. EXISTING DEVICES TO REMAIN. PROVIDE NEW CABLING AND CONDUIT AS NEEDED.
D. EXISTING DEVICES TO BE DEMOLISHED BY THE CONTRACTOR.
R. EXISTING DEVICES TO BE REPLACED WITH NEW BY THE CONTRACTOR.
N. NEW DEVICES TO BE PROVIDED AND INSTALLED BY THE CONTRACTOR.
ALL HEIGHTS ARE TO CENTER OF DEVICE UNLESS NOTED OTHERWISE. HEIGHTS INDICATED IN PLANS SHALL SUPERSEDE THOSE LISTED HERE.

KEY PLAN

SCALE: NO SCALE


SCOPE OUTLINE
AREA OF WORK


WALL RATING LEGEND

- 1 HR - FIRE SEPARATION
- 2 HR - FIRE SEPARATION
- SMOKE RESISTIVE HAZARDOUS AREA

**FULLY SPRINKLERED
100% CONSTRUCTION DOCUMENTS**

C:\Users\pneuschwander\Documents\E_22-038_Vest_Palm_Beach_Regional_PAMNS_FI_pneuschwander.rvt
12/14/2022 4:10:30 PM
VA FORM 08-6231
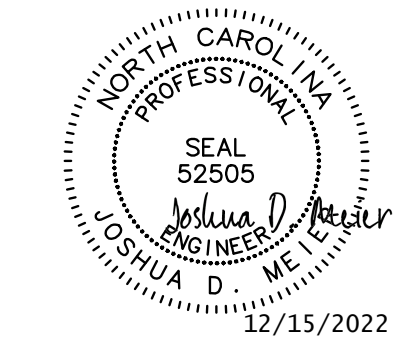
#	Revisions:	Date	CONSULTANTS:	 Glenn D Albright III BICS ID # 363972 Expires 12/31/24 RCDD 12/15/2022	 Glenn D Albright III Professional Engineer North Carolina 12/15/2022	PROJECT MANAGER Headquarters: Apogee Consulting Group, P.A. 1151 Kildaire Farm Road, Suite 120 Cary, North Carolina 27511 www.acg-pa.com 919-858-7420	ACG Project Number 22-038	Office of Construction and Facilities Management VA U.S. Department of Veterans Affairs	Drawing Title FOURTH FLOOR NW PAMNS	Project Title REMOVE AND REPLACE PUBLIC ADDRESS SYSTEM	VA PROJECT NUMBER 548-22-100	
									Location WEST PALM BEACH VAMC 7305 NORTH MILITARY TRAIL WEST PALM BEACH FL, 33410-6400	Approved	Building Number #	Drawing Number T-143
									Date DECEMBER 14, 2022	Checked JDM	Drawn HT	Dwg 21 of 32

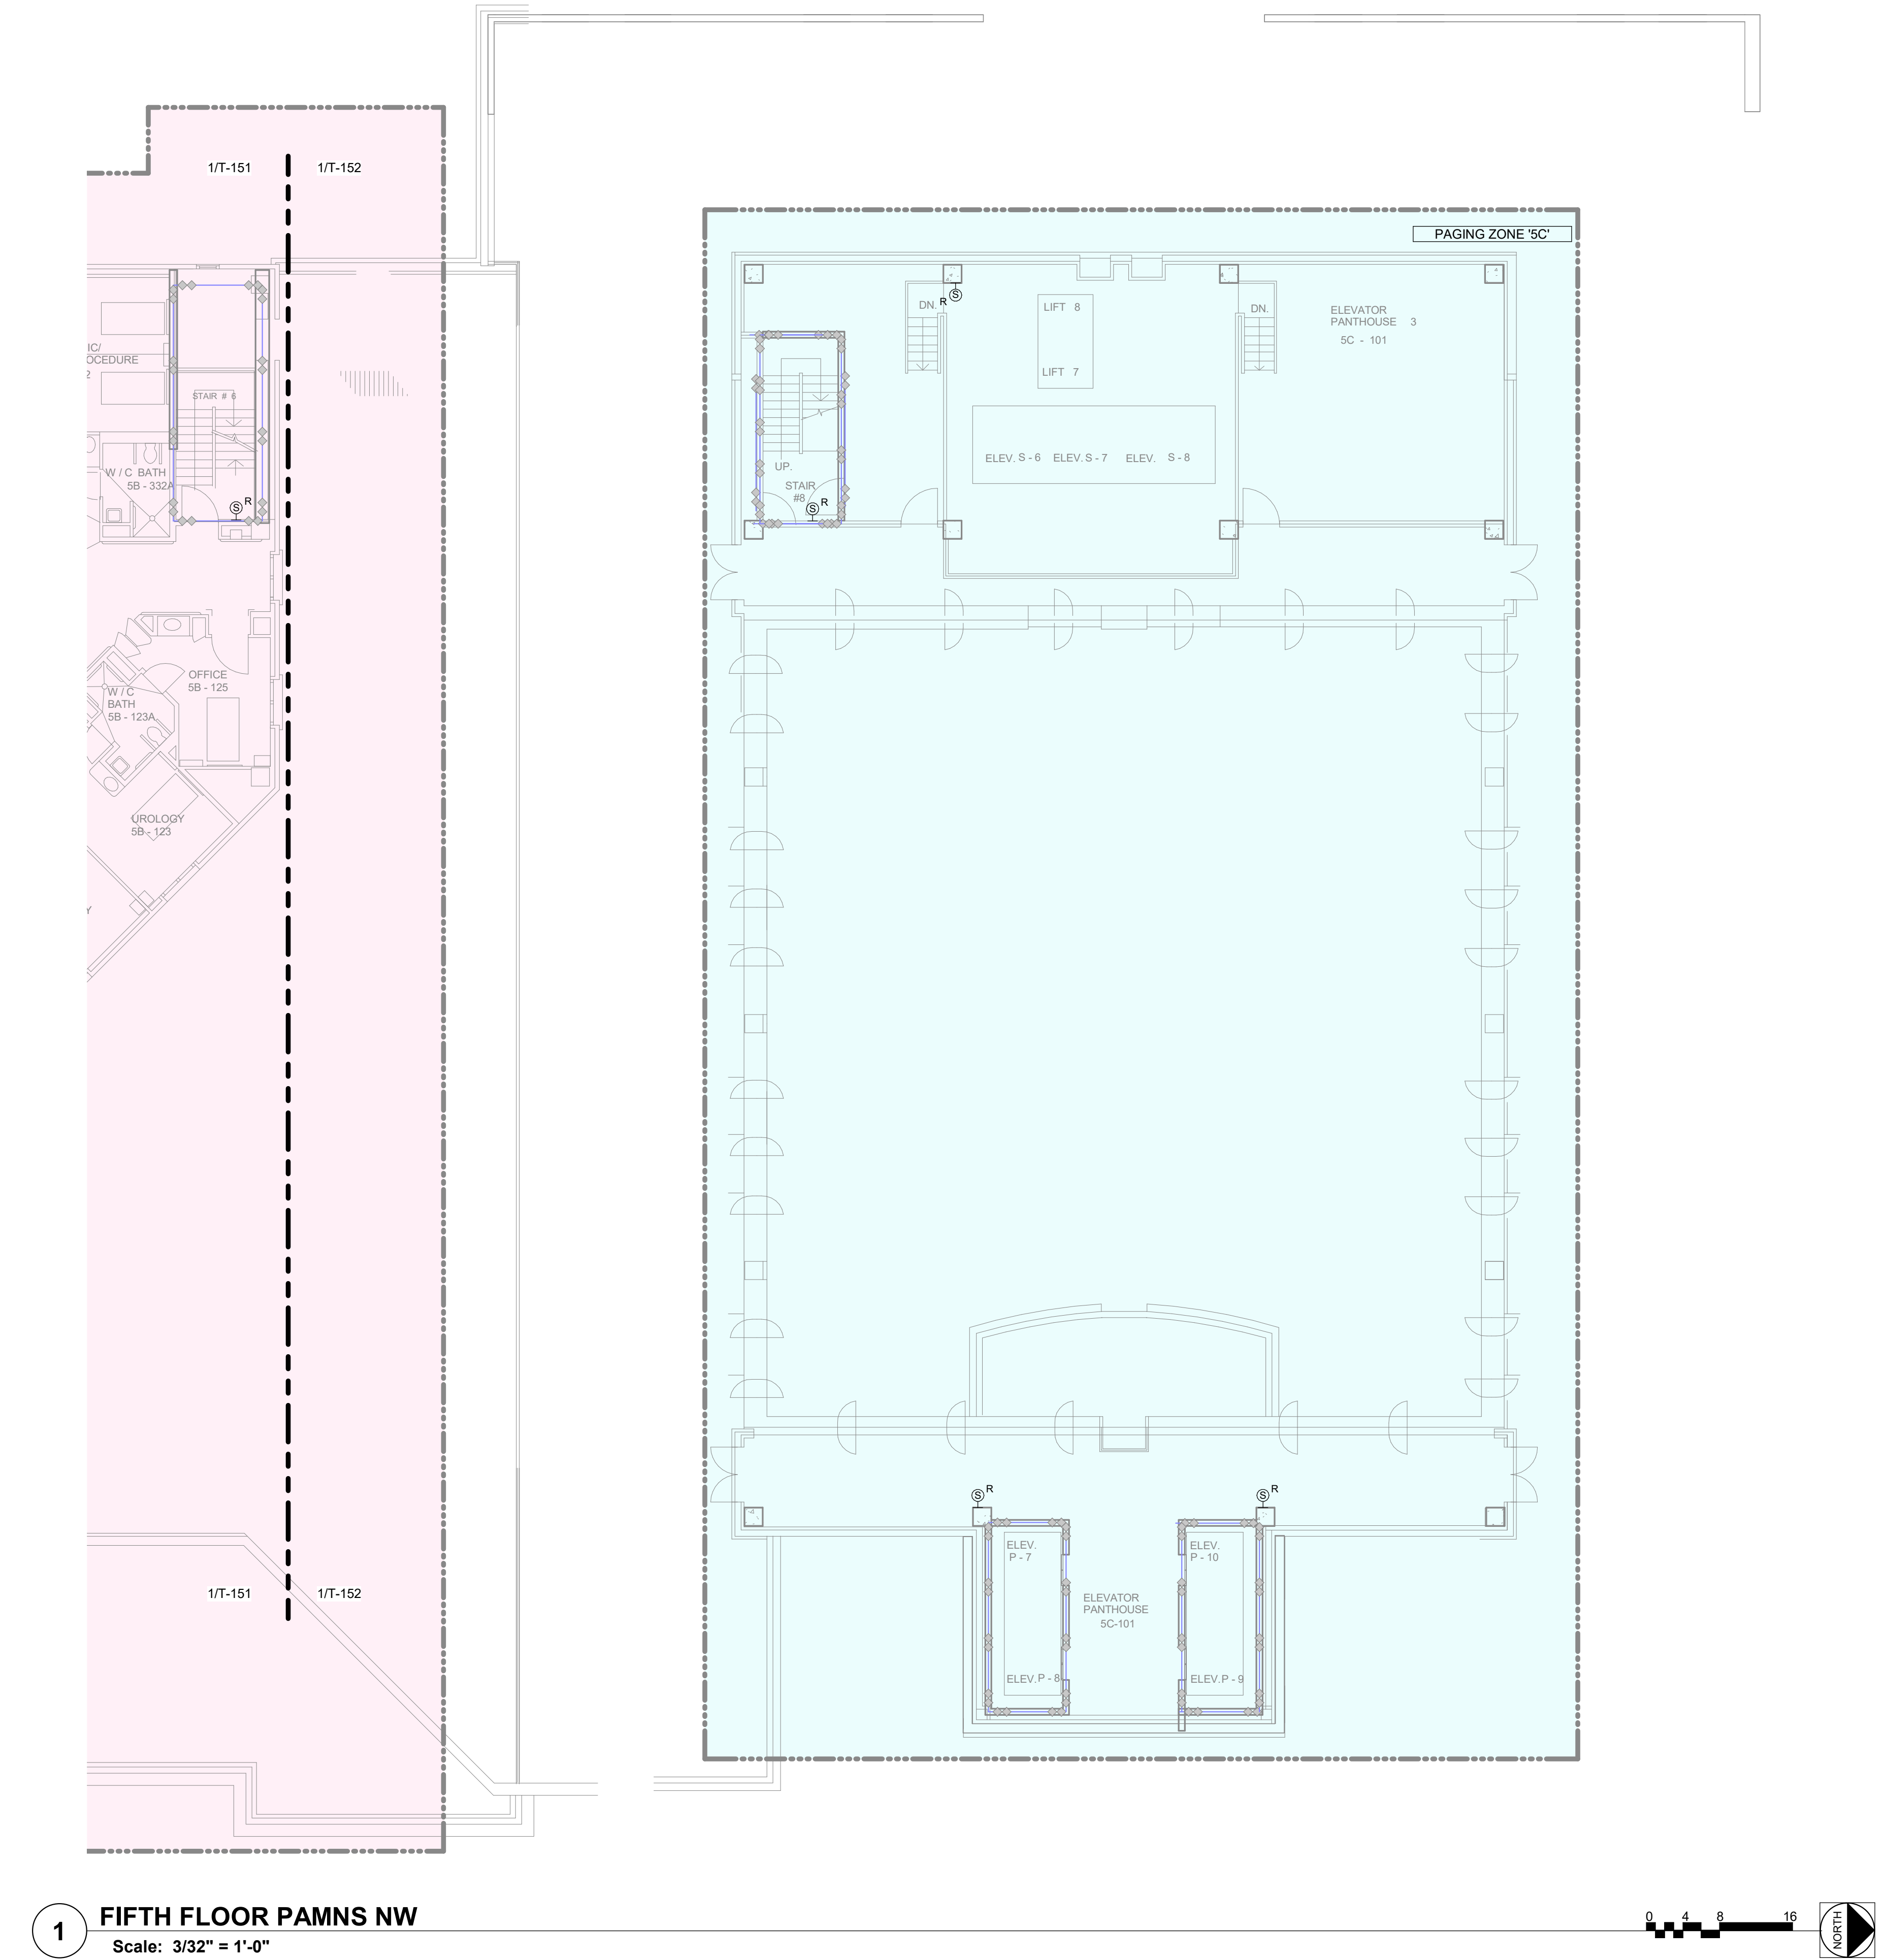

1 FIFTH FLOOR PAMNS NW
Scale: 3/32" = 1'-0"


- SHEET NOTES:**
- A. PROVIDE PAMNS DEVICES AT LOCATIONS INDICATED ON PLANS. PROVIDE WIRING AND CIRCUIT AS INDICATED ON DETAILS.
 - B. ALL PAMN WIRING SHALL BE CONCEALED IN WALLS, IN RACEWAY OR AND ABOVE THE CEILING IN CONDUIT.
 - C. PAMN WIRING IN UNFINISHED AREAS SHALL BE IN SURFACE MOUNTED RACEWAY (MECH. ROOM, ROOMS WITH NO CEILINGS.)
 - D. ALL CEILING SPEAKERS SHALL BE SET AT 1/2 WATT UNLESS NOTED OTHERWISE.
 - E. ALL WALL MOUNTED SPEAKERS SHALL BE SET AT 4 WATTS UNLESS NOTED OTHERWISE.
 - F. CONTRACTOR RESPONSIBLE FOR PROVIDING AND INSTALLING FIRE SLEEVES FOR FIREWALL. CONTRACTOR SHALL ADEQUATELY REPAIR ANY FIREWALL PENETRATIONS.

- KEY NOTES:**
- 1 LOCATION OF VERTICAL RISER IN LIFT SHAFT. REF. T-601
 - 2 VOLUME CONTROL FOR NURSE STATION 5A-210, WAITING ROOM 5A-101 & CORRIDORS 5A-C1, 5A-C2, 5A-C4, 5A-C7.
 - 3 VOLUME CONTROL FOR NURSE STATION 5B-211, WAITING ROOM 5B-101 & CORRIDORS 5B-C1, 5B-C2, 5B-C4, 5B-C7.

ABBREVIATED SYMBOL LEGEND

SYMBOL	HEIGHT	DESCRIPTION
Ⓢ	CEILING	CEILING MOUNTED SPEAKER
Ⓢ	96"	WALL MOUNTED SPEAKER
Ⓢ	AS NOTED	WALL MOUNTED HORN
Ⓢ	48"	VOLUME CONTROL
Ⓢ	48"	PAGING CONSOLE
Ⓢ	FLOOR	PAGING CABINET


DEVICES WITH THE FOLLOWING TAGS ARE AS INDICATED:
E: EXISTING DEVICES TO REMAIN. PROVIDE NEW CABLING AND CONDUIT AS NEEDED.
D: EXISTING DEVICES TO BE DEMOLISHED BY THE CONTRACTOR.
R: EXISTING DEVICES TO BE REPLACED WITH NEW BY THE CONTRACTOR.
N: NEW DEVICES TO BE PROVIDED AND INSTALLED BY THE CONTRACTOR.
ALL HEIGHTS ARE TO CENTER OF DEVICE UNLESS NOTED OTHERWISE. HEIGHTS INDICATED IN PLANS SHALL SUPERSEDE THOSE LISTED HERE.

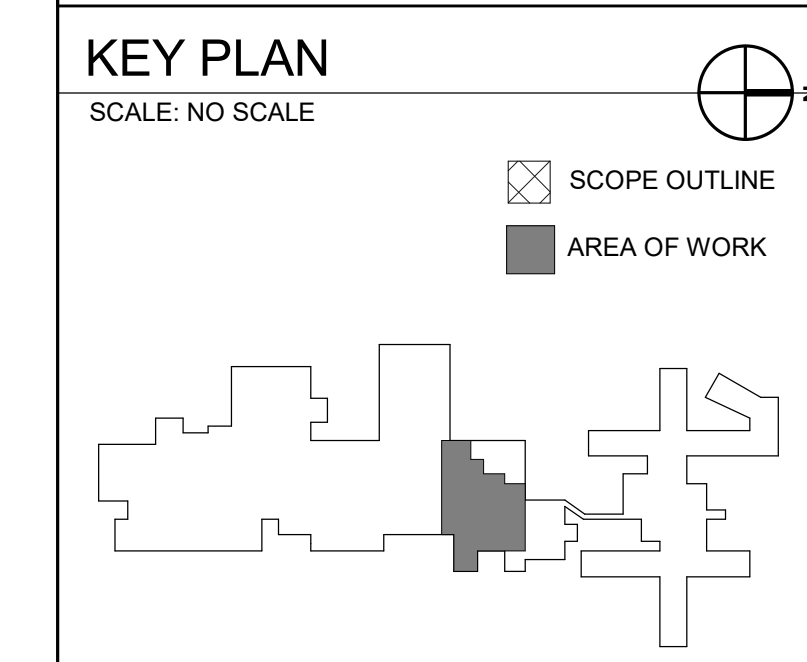


WALL RATING LEGEND

1 HR - FIRE SEPARATION
2 HR - FIRE SEPARATION
SMOKE RESISTIVE HAZARDOUS AREA

**FULLY SPRINKLERED
100% CONSTRUCTION DOCUMENTS**
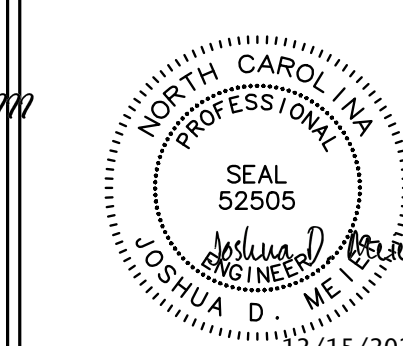
#	Revisions:	Date	CONSULTANTS:	 REGISTERED COMMUNICATIONS DISTRICT DESIGN Bicsi Glenn D Altshrock III BICS ID # 363972 EXPIRES 12-31-24 RCDD 12/15/2022	 NORTH CAROLINA PROFESSIONAL ENGINEER SEAL 52505 JOSHUA D. WILKINS 12/15/2022	PROJECT MANAGER Headquarters: Apogee Consulting Group, P.A. 1151 Kildaire Farm Road, Suite 120 Cary, North Carolina 27511 www.acg-pa.com 919-858-7420 © COPYRIGHT Apogee Consulting Group, P.A.	ACG Project Number 22-038	Office of Construction and Facilities Management VA U.S. Department of Veterans Affairs	Drawing Title FIFTH FLOOR PAMNS NW	Project Title REMOVE AND REPLACE PUBLIC ADDRESS SYSTEM	VA PROJECT NUMBER 548-22-100	
									Location WEST PALM BEACH VAMC 7305 NORTH MILITARY TRAIL WEST PALM BEACH FL, 33410-6400	Approved	Building Number #	Drawing Number T-152
									Date DECEMBER 14, 2022	Checked JDM	Drawn HT	Dwg 23 of 32

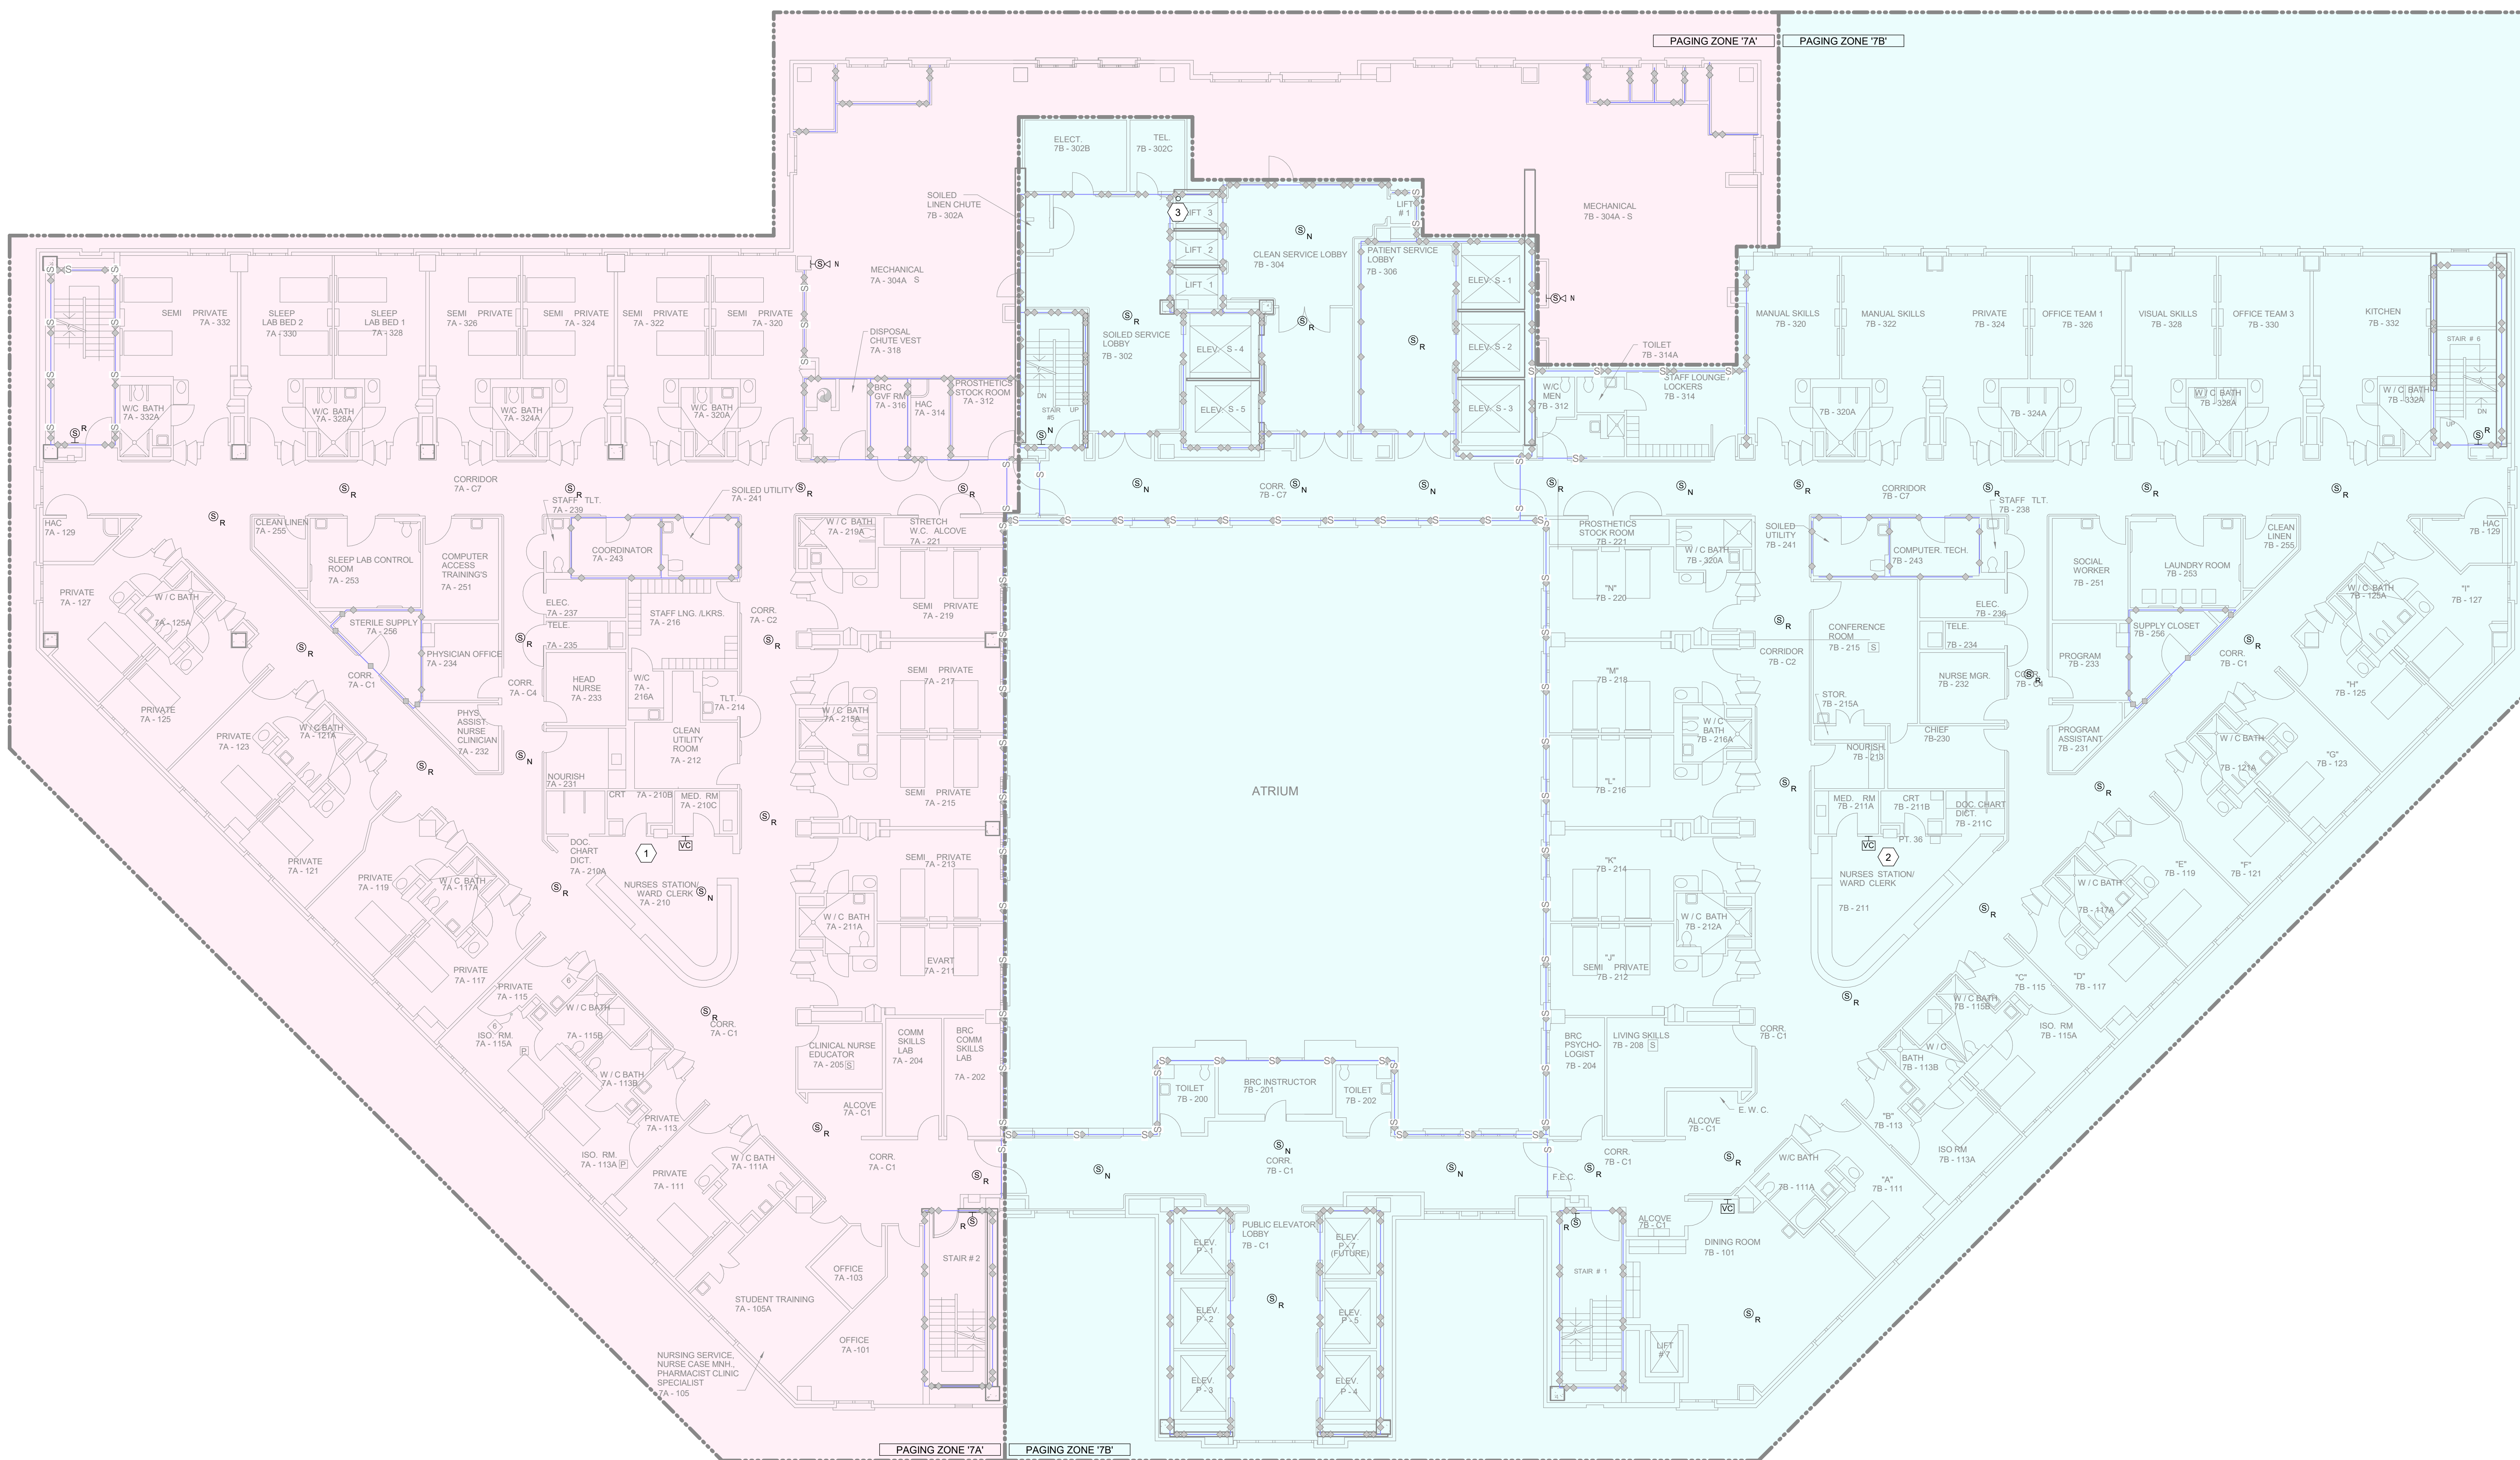

1 SEVENTH FLOOR PAMNS
Scale: 3/32" = 1'-0"

16  FULLY SPRINKLERED
100% CONSTRUCTION DOCUMENTS

SHEET NOTES:

- A. PROVIDE PAMMS DEVICES AT LOCATIONS INDICATED ON PLANS. PROVIDE WIRING AND CIRCUIT AS INDICATED ON DETAILS.
- B. ALL PAMM WIRING SHALL BE CONCEALED IN WALLS, IN RACEWAY OR AND ABOVE THE CEILING IN CONDUIT.
- C. PAMM WIRING IN UNFINISHED AREAS SHALL BE IN SURFACE MOUNTED RACEWAY (MECH. ROOM, ROOMS WITH NO CEILINGS.)
- D. ALL CEILING SPEAKERS SHALL BE SET AT 1/2 WALL UNLESS NOTED OTHERWISE.
- E. ALL WALL MOUNTED SPEAKERS SHALL BE SET AT 4 WALLS UNLESS NOTED OTHERWISE.
- F. CONTRACTOR RESPONSIBLE FOR PROVIDING AND INSTALLING FIRE SLEEVES FOR FIREWALL. CONTRACTOR SHALL ADEQUATELY REPAIR ANY FIREWALL PENETRATIONS.

KEY NOTES

- 1 VOLUME CONTROL FOR NURSE STATION
7A-210, WAITING ROOM 7A-101 & CORRIDORS
7A-C1, 7A-C2, 7A-C4, 7A-C7.
- 2 VOLUME CONTROL FOR NURSE STATION
7B-211, WAITING ROOM 7B-101 & CORRIDORS
7B-C1, 7B-C2, 7B-C4, 7B-C7.
- 3 LOCATION OF VERTICAL RISER IN LIFT
SHAFT. RFF. T-801


**ABBREVIATED SYMBOL
LEGEND**

SYMBOL	HEIGHT	DESCRIPTION
	CEILING	CEILING MOUNTED SPEAKER
	96"	WALL MOUNTED SPEAKER
	AS NOTED	WALL MOUNTED HORN
	48"	VOLUME CONTROL
	48"	PAGING CONSOLE
	FLOOR	PAGING CABINET


DEVICES WITH THE FOLLOWING TAGS ARE AS INDICATED:
C: EXISTING DEVICES TO REMAIN. PROVIDE NEW CABLING AND CONDUIT AS NEEDED.
D: EXISTING DEVICES TO BE DEMOLISHED BY THE CONTRACTOR.
R: EXISTING DEVICES TO BE REPLACED WITH NEW BY THE CONTRACTOR.
N: NEW DEVICES TO BE PROVIDED AND INSTALLED BY THE CONTRACTOR.
ALL DEVICES ARE TO BE IDENTIFIED BY DEVICE UNLESS NOTED OTHERWISE. HEIGHTS INDICATED IN PLANS SHALL SUPERSEDE THOSE LISTED HERE.

KEY PLAN

SCALE: NO SCAL

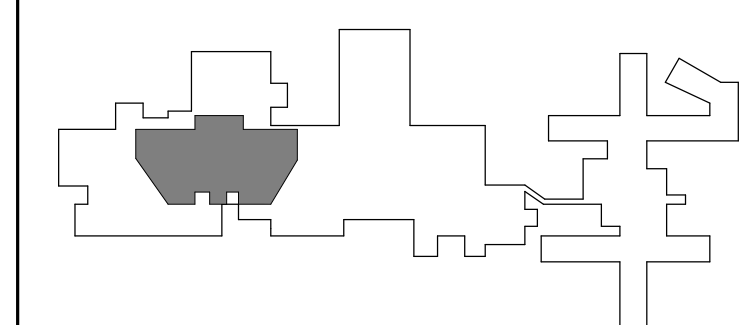

WALL RATING LEGEND

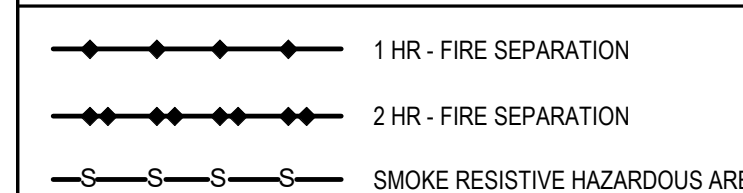


FULLY SPRINKLERED
CONSTRUCTION DOCUMENTS

CONSULTANTS:

#	Revisions:	Date



PROJECT MANAGER

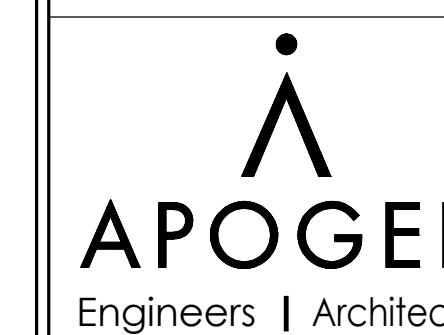

Headquarters:
Apogee Consulting Group, P.A.
1151 Kildaire Farm Road, Suite 120
Cary, North Carolina 27511

ACG Project Number	22-03
--------------------	-------

Office of

Office of
Construction
and Facilities
Management

VA | U.S. Department
of Veterans Affairs

Drawing Title	SEVENTH FLOOR PAMNS
---------------	---------------------

Location	WEST PALM BEACH VAMC 7305 NORTH MILITARY TRAIL WEST PALM BEACH FL, 33410-6401
----------	---

Project Title	REMOVE AND REPLACE PUBLIC ADDRESS SYSTEM
---------------	---

	Approved
	Date DECEMBER 14, 202

2	Checked JDM	Drawn HT
---	----------------	-------------

1	VA PROJECT NUMBER 548-22-100
	Building Number #
	Drawing Number T-171

Dwg. 25 of 32

SHEET NOTES:

- A. PROVIDE PAMNS DEVICES AT LOCATIONS INDICATED ON PLANS. PROVIDE WIRING AND CIRCUIT AS INDICATED ON DETAILS.
- B. ALL PAMN WIRING SHALL BE CONCEALED IN WALLS, IN RACEWAY OR AND ABOVE THE CEILING IN CONDUIT.
- C. PAMN WIRING IN UNFINISHED AREAS SHALL BE IN SURFACE MOUNTED RACEWAY (MECH. ROOM, ROOMS WITH NO CEILINGS.)
- D. ALL CEILING SPEAKERS SHALL BE SET AT 1/2 WATT UNLESS NOTED OTHERWISE.
- E. ALL WALL MOUNTED SPEAKERS SHALL BE SET AT 4 WATTS UNLESS NOTED OTHERWISE.
- F. CONTRACTOR RESPONSIBLE FOR PROVIDING AND INSTALLING FIRE SLEEVES FOR FIREWALL. CONTRACTOR SHALL ADEQUATELY REPAIR ANY FIREWALL PENETRATIONS.

KEY NOTES:

- 1 VOLUME CONTROL FOR RECEPTION 9A-210, WAITING 9A-202, STAFF LOUNGE 9A-356 & CORRIDORS 9A-C1, 9A-C1A, 9A-C1B, 9A-C1C, 9A-C1D, 9A-C1E, 9A-C2, 9A-C7, 9A-C7A, 9A-C7B, 9A-C7C.


ABBREVIATED SYMBOL LEGEND

SYMBOL	HEIGHT	DESCRIPTION
	CEILING	CEILING MOUNTED SPEAKER
	90°	WALL MOUNTED SPEAKER
	AS NOTED	WALL MOUNTED HORN
	48"	VOLUME CONTROL
	48"	PAGING CONSOLE
	FLOOR	PAGING CABINET

DEVICES WITH THE FOLLOWING TAGS ARE AS INDICATED:
E: EXISTING DEVICES TO REMAIN. PROVIDE NEW CABLING AND CONDUIT AS NEEDED.
D: EXISTING DEVICES TO BE DEMOLISHED BY THE CONTRACTOR.
R: EXISTING DEVICES TO BE REPLACED WITH NEW BY THE CONTRACTOR.
N: NEW DEVICES TO BE PROVIDED AND INSTALLED BY THE CONTRACTOR.
ALL HEIGHTS ARE TO CENTER OF DEVICE UNLESS NOTED OTHERWISE. HEIGHTS INDICATED IN PLANS SHALL SUPERSEDE THOSE LISTED HERE.

KEY PLAN

SCALE: NO SCALE

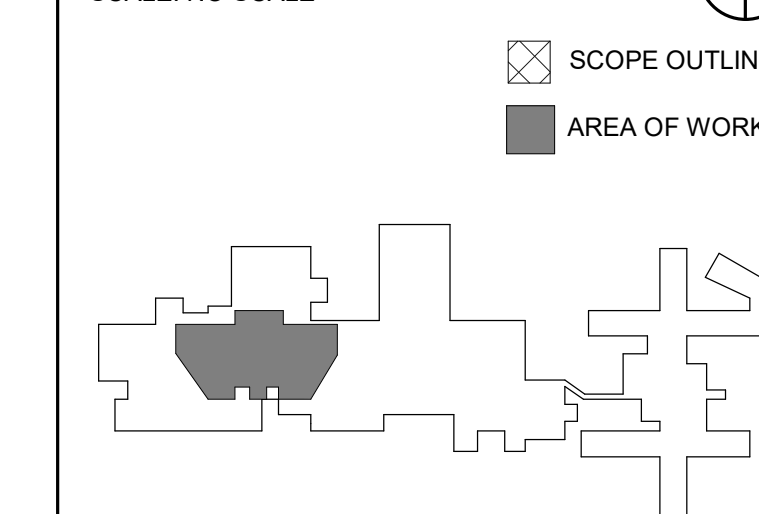

WALL RATING LEGEND

	1 HR - FIRE SEPARATION
	2 HR - FIRE SEPARATION
	SMOKE RESISTIVE HAZARDOUS AREA

FULLY SPRINKLERED
100% CONSTRUCTION DOCUMENTS

1 NINTH FLOOR PAMNS

Scale: 3/32" = 1'-0"



CONSULTANTS:



PROJECT MANAGER
ACG Project Number 22-038
Headquarters:
Apogee Consulting Group, P.A.
1151 Kildaire Farm Road, Suite 120
Cary, North Carolina 27511
www.acg-pa.com 919-858-7420


Office of
Construction
and Facilities
Management
VA U.S. Department
of Veterans Affairs

Drawing Title
NINTH FLOOR PAMNS
Location
**WEST PALM BEACH VAMC
7305 NORTH MILITARY TRAIL
WEST PALM BEACH FL, 33410-6400**


Project Title
**REMOVE AND REPLACE
PUBLIC ADDRESS SYSTEM**
Approved
Date
DECEMBER 14, 2022
Checked
JDM
Drawn
HT

VA PROJECT NUMBER
548-22-100
Building Number

Drawing Number
T-191
Dwg 27 of 32

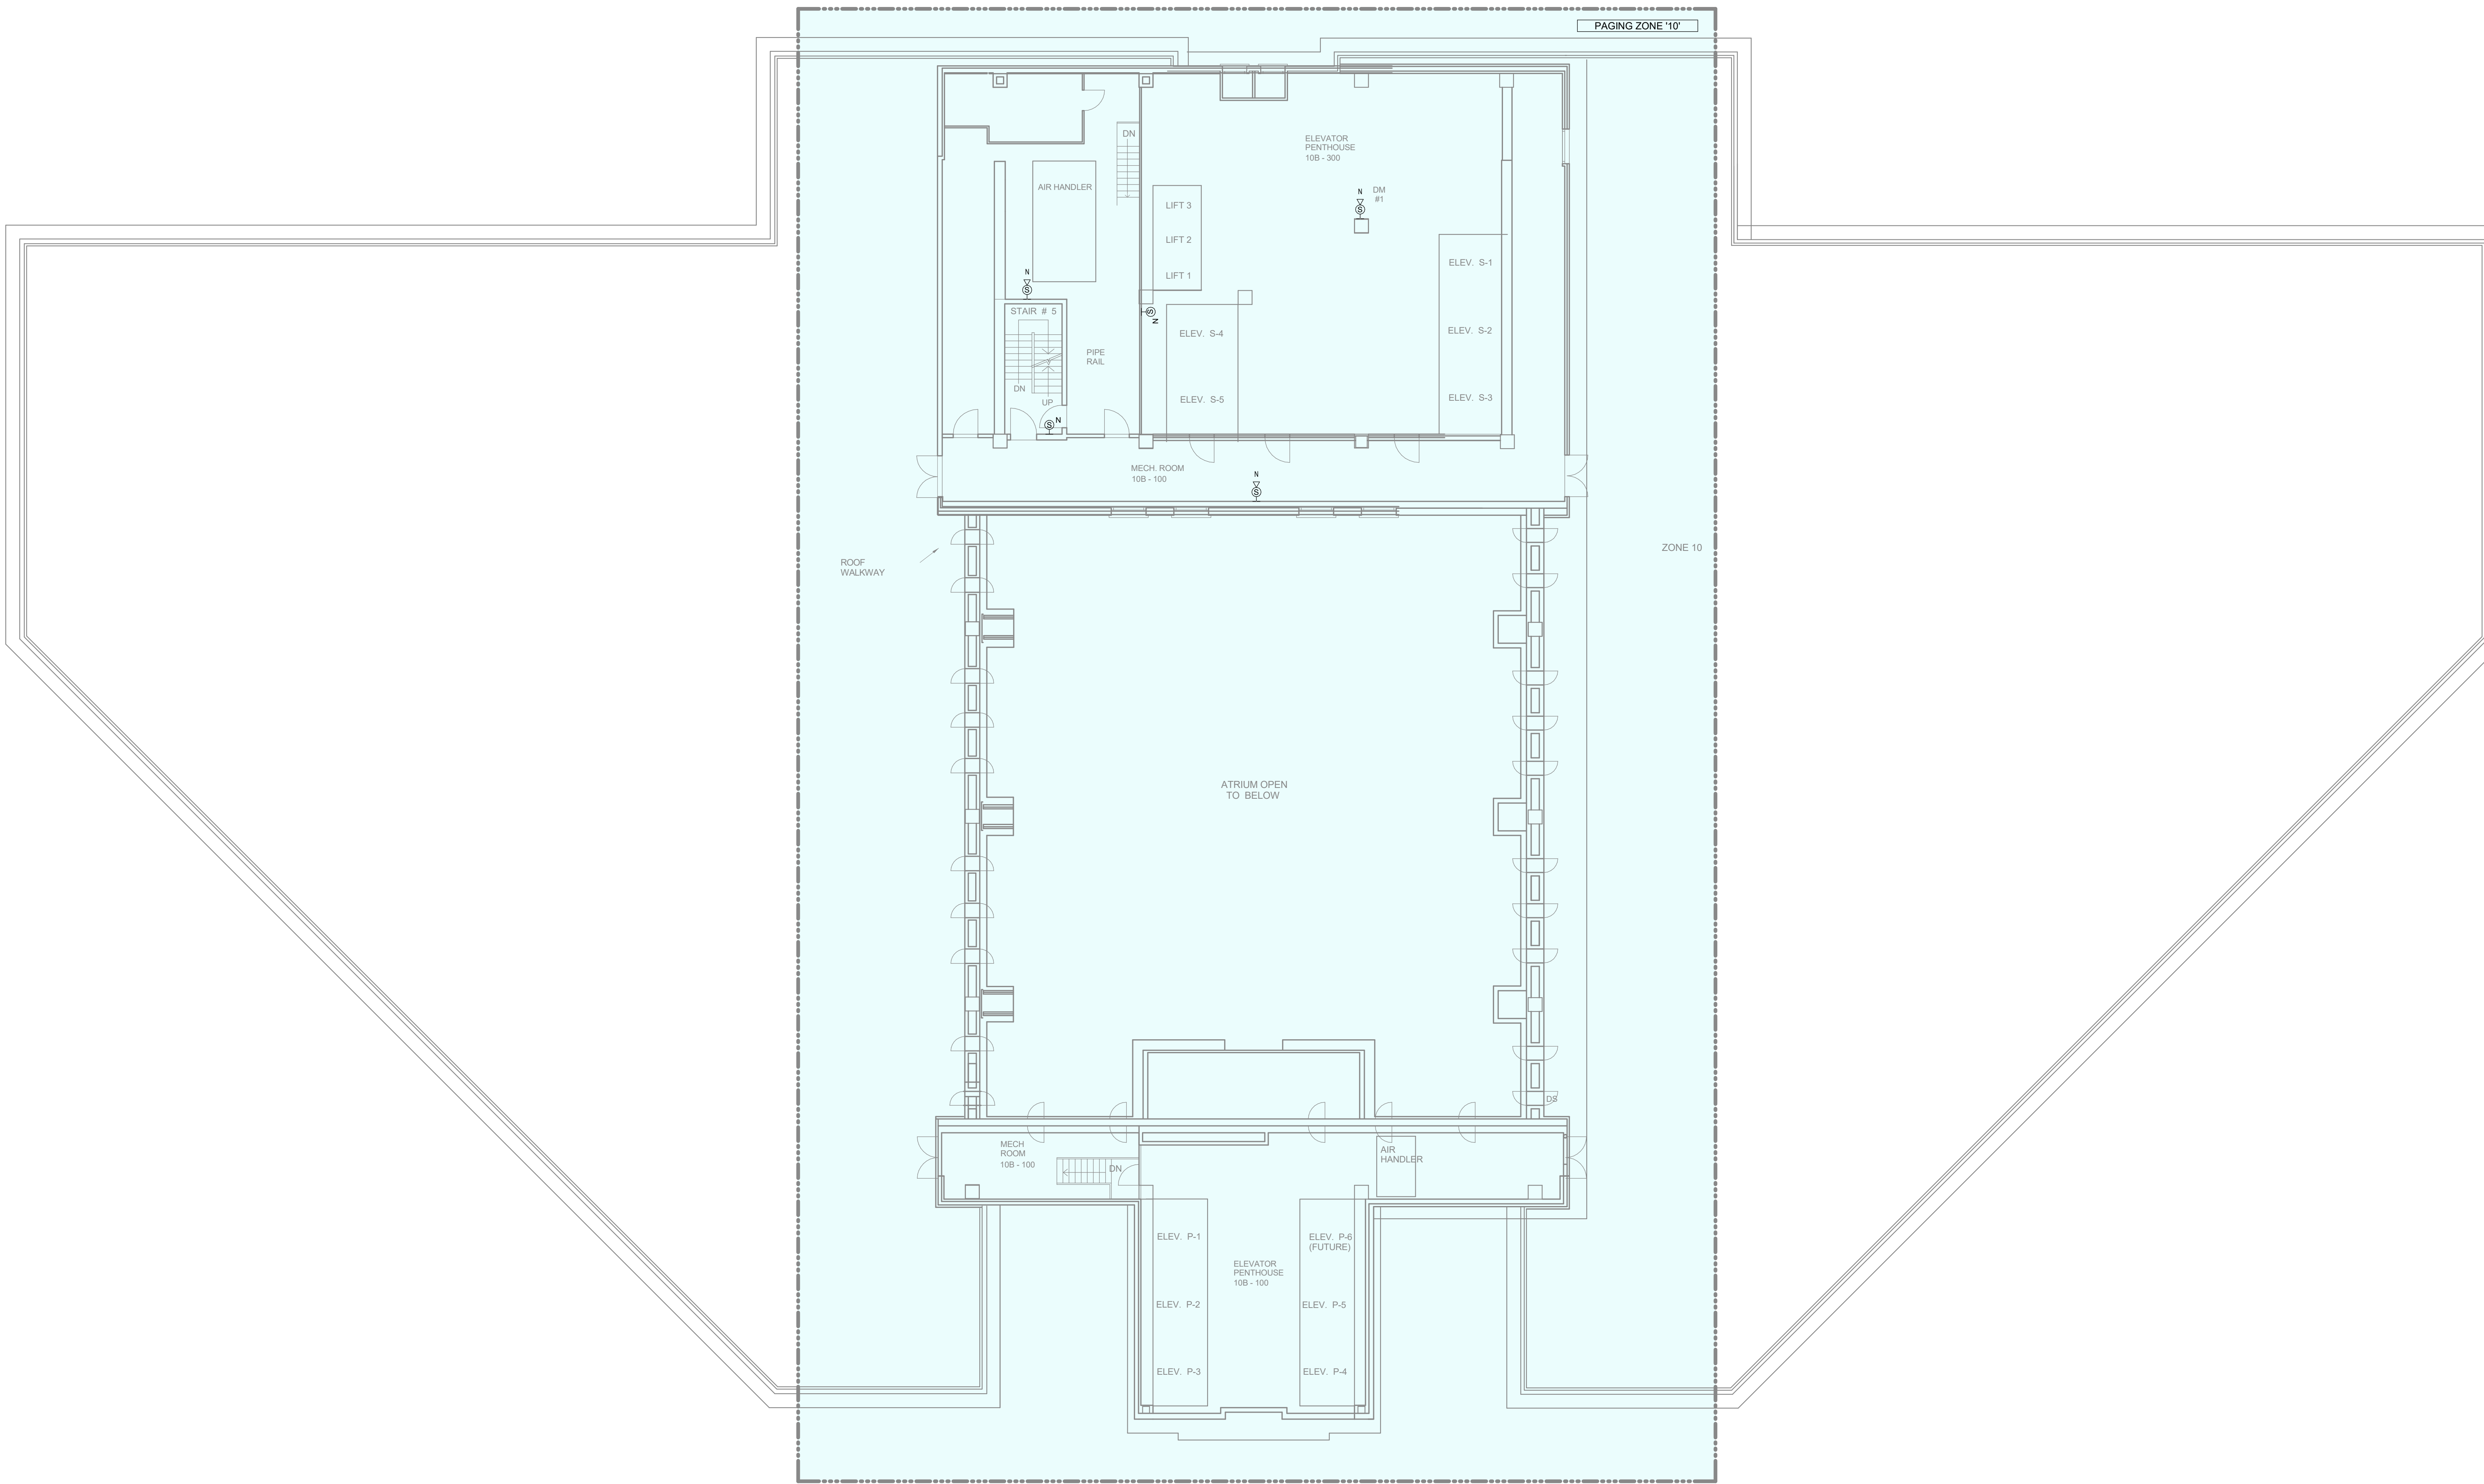

1 TENTH FLOOR PAMNS
Scale: 3/32" = 1'-0"

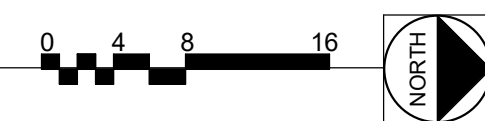

- SHEET NOTES:**
- A. PROVIDE PAMNS DEVICES AT LOCATIONS INDICATED ON PLANS. PROVIDE WIRING AND CIRCUIT AS INDICATED ON DETAILS.
 - B. ALL PAMN WIRING SHALL BE CONCEALED IN WALLS, IN RACEWAY OR AND ABOVE THE CEILING IN CONDUIT.
 - C. PAMN WIRING IN UNFINISHED AREAS SHALL BE IN SURFACE MOUNTED RACEWAY (MECH. ROOM, ROOMS WITH NO CEILINGS.)
 - D. ALL CEILING SPEAKERS SHALL BE SET AT 1/2 WATT UNLESS NOTED OTHERWISE.
 - E. ALL WALL MOUNTED SPEAKERS SHALL BE SET AT 4 WATTS UNLESS NOTED OTHERWISE.
 - F. CONTRACTOR RESPONSIBLE FOR PROVIDING AND INSTALLING FIRE SLEEVES FOR FIREWALL. CONTRACTOR SHALL ADEQUATELY REPAIR ANY FIREWALL PENETRATIONS.

- KEY NOTES:**
- 1 VOLUME CONTROL FOR RECEPTION 9A-210, WAITING 9A-202, STAFF LOUNGE 9A-356 & CORRIDORS 9A-C1, 9A-C1A, 9A-C1B, 9A-C1C, 9A-C1D, 9A-C1E, 9A-C2, 9A-C7, 9A-C7A, 9A-C7B, 9A-C7C.

ABBREVIATED SYMBOL LEGEND

SYMBOL	HEIGHT	DESCRIPTION
	CEILING	CEILING MOUNTED SPEAKER
	96"	WALL MOUNTED SPEAKER
	AS NOTED	WALL MOUNTED HORN
	48"	VOLUME CONTROL
	48"	PAGING CONSOLE
	FLOOR	PAGING CABINET

DEVICES WITH THE FOLLOWING TAGS ARE AS INDICATED:
E: EXISTING DEVICES TO REMAIN. PROVIDE NEW CABLING AND CONDUIT AS NEEDED.
D: EXISTING DEVICES TO BE DEMOLISHED BY THE CONTRACTOR.
R: EXISTING DEVICES TO BE REPLACED WITH NEW BY THE CONTRACTOR.
N: NEW DEVICES TO BE PROVIDED AND INSTALLED BY THE CONTRACTOR.
ALL HEIGHTS ARE TO CENTER OF DEVICE UNLESS NOTED OTHERWISE. HEIGHTS INDICATED IN PLANS SHALL SUPERSEDE THOSE LISTED HERE.

KEY PLAN
SCALE: NO SCALE



SCOPE OUTLINE
 AREA OF WORK

WALL RATING LEGEND

	1 HR - FIRE SEPARATION
	2 HR - FIRE SEPARATION
	SMOKE RESISTIVE HAZARDOUS AREA


**FULLY SPRINKLERED
100% CONSTRUCTION DOCUMENTS**

CONSULTANTS:				PROJECT MANAGER		ACG Project Number 22-038		Office of Construction and Facilities Management	Drawing Title TENTH FLOOR PAMNS		Project Title REMOVE AND REPLACE PUBLIC ADDRESS SYSTEM		VA PROJECT NUMBER 548-22-100		
				Headquarters: Apogee Consulting Group, P.A. 1151 Kildaire Farm Road, Suite 120 Cary, North Carolina 27511		www.acg-pa.com 919-858-7420			Location WEST PALM BEACH VAMC 7305 NORTH MILITARY TRAIL WEST PALM BEACH FL, 33410-6400		Approved Date DECEMBER 14, 2022		Checked JDM		Drawing Number T-192 Dwg 28 of 32
# Revisions:		Date													

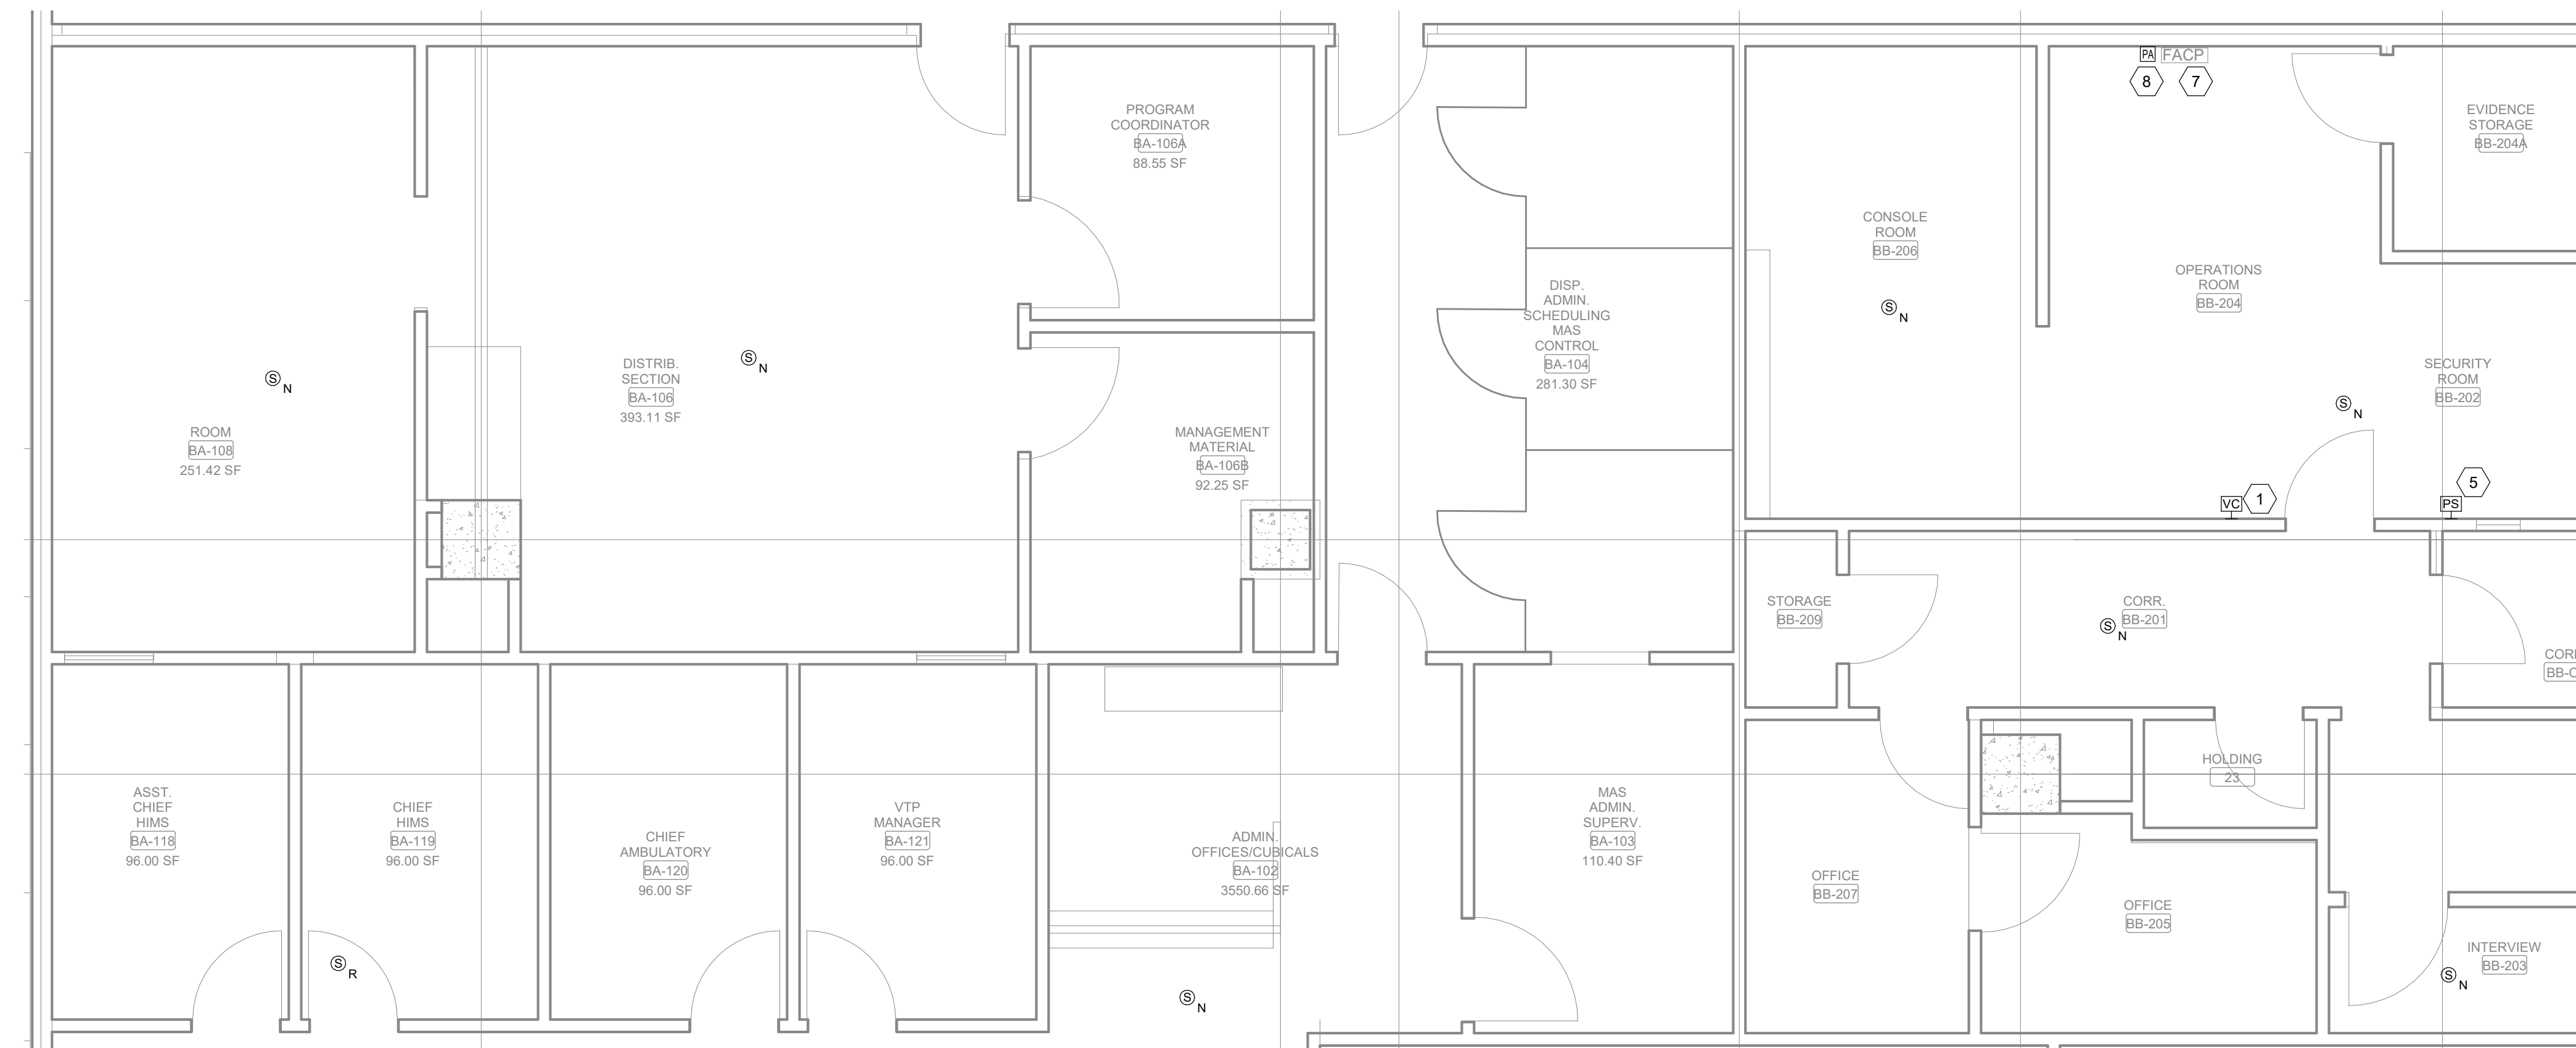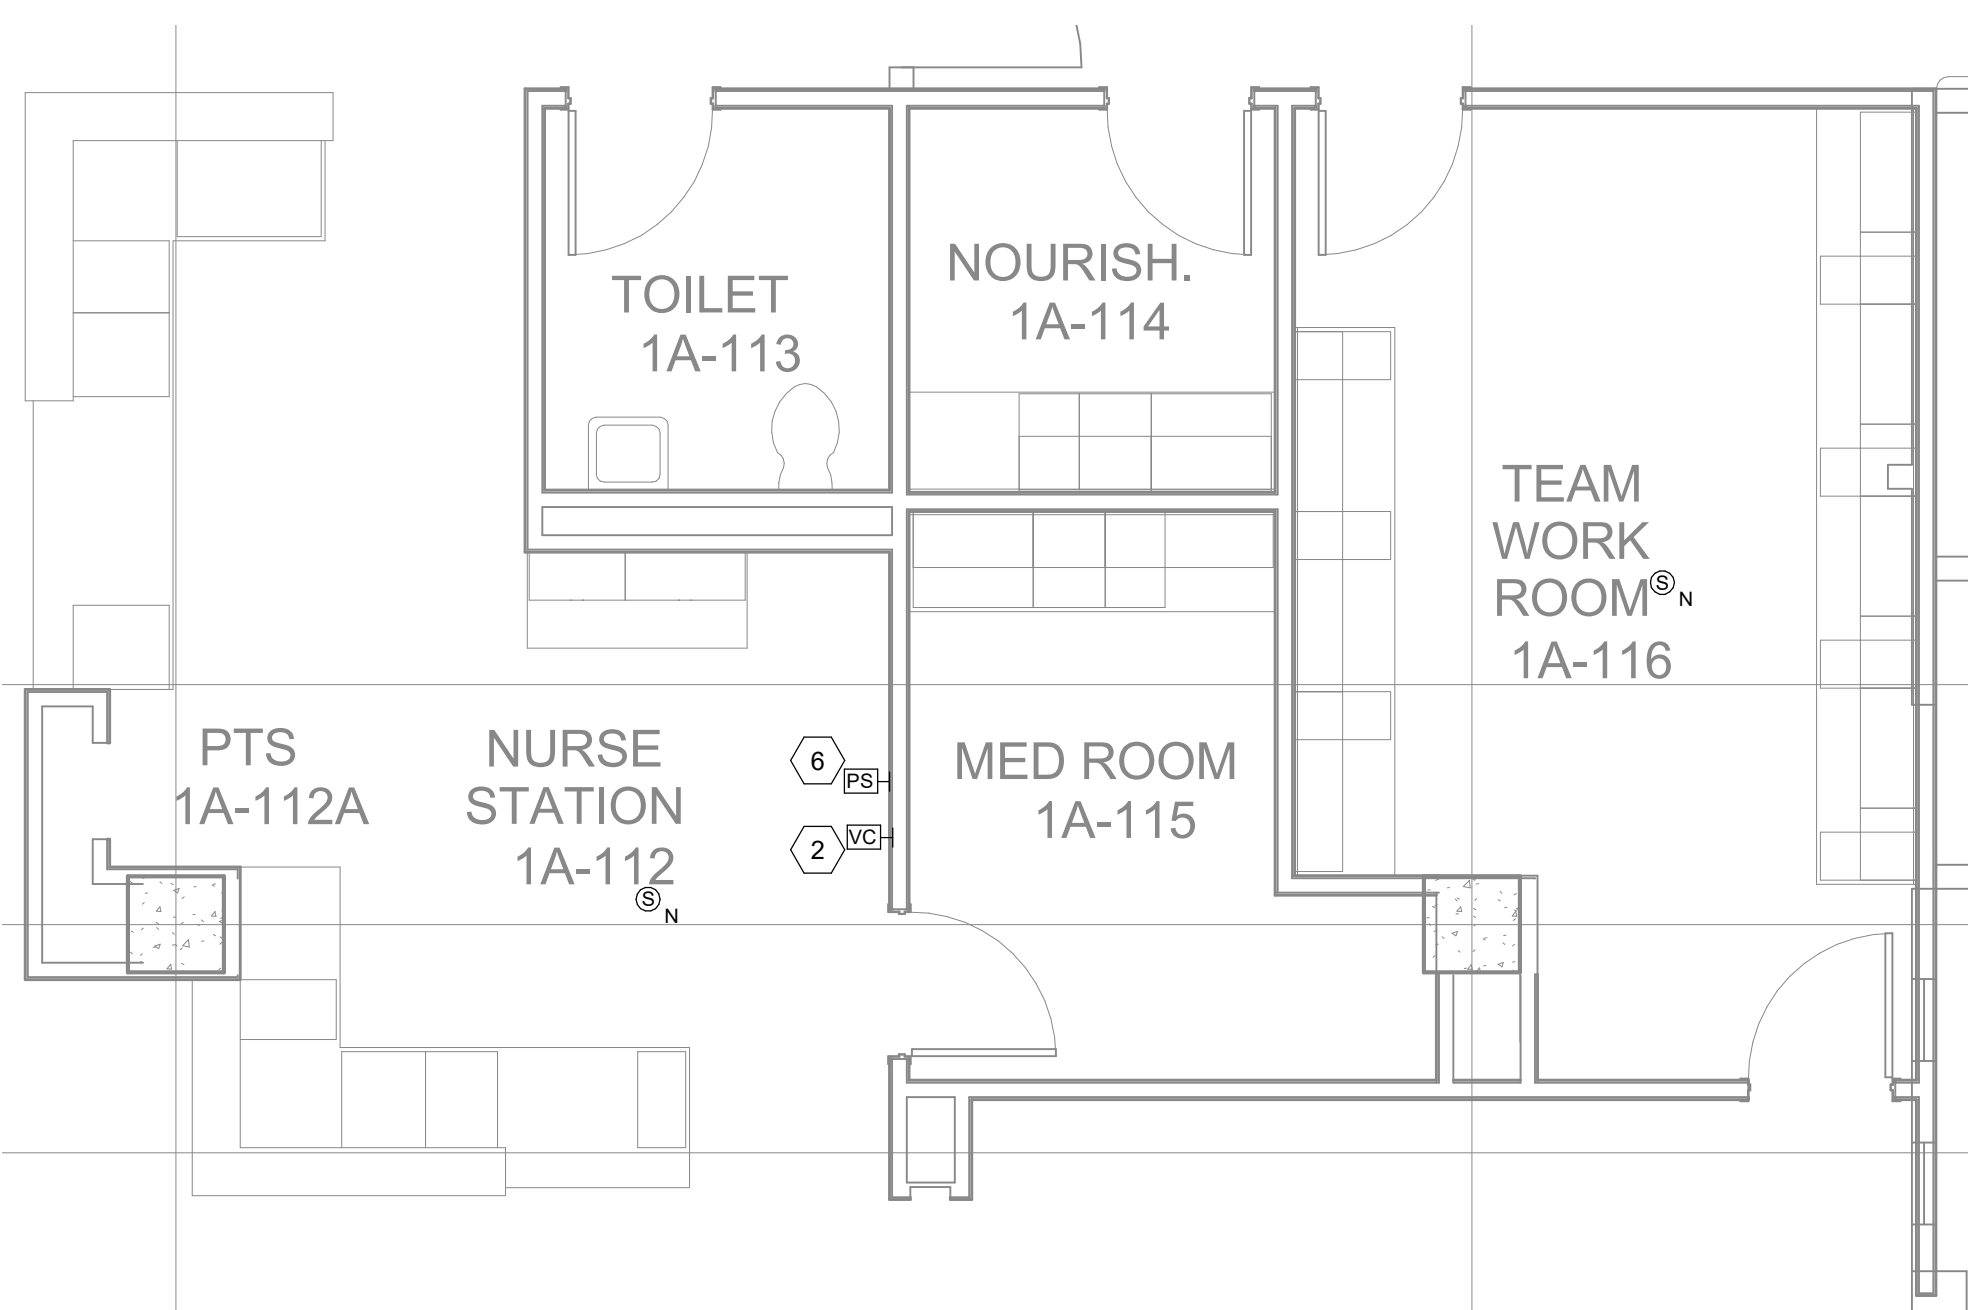


4 FIRST FLOOR ENLARGEMENT - ED NURSES STATION
Scale: 1/4" = 1'-0"

1 BASEMENT ENLARGEMENT - POLICE CENTER
Scale: 1/4" = 1'-0"

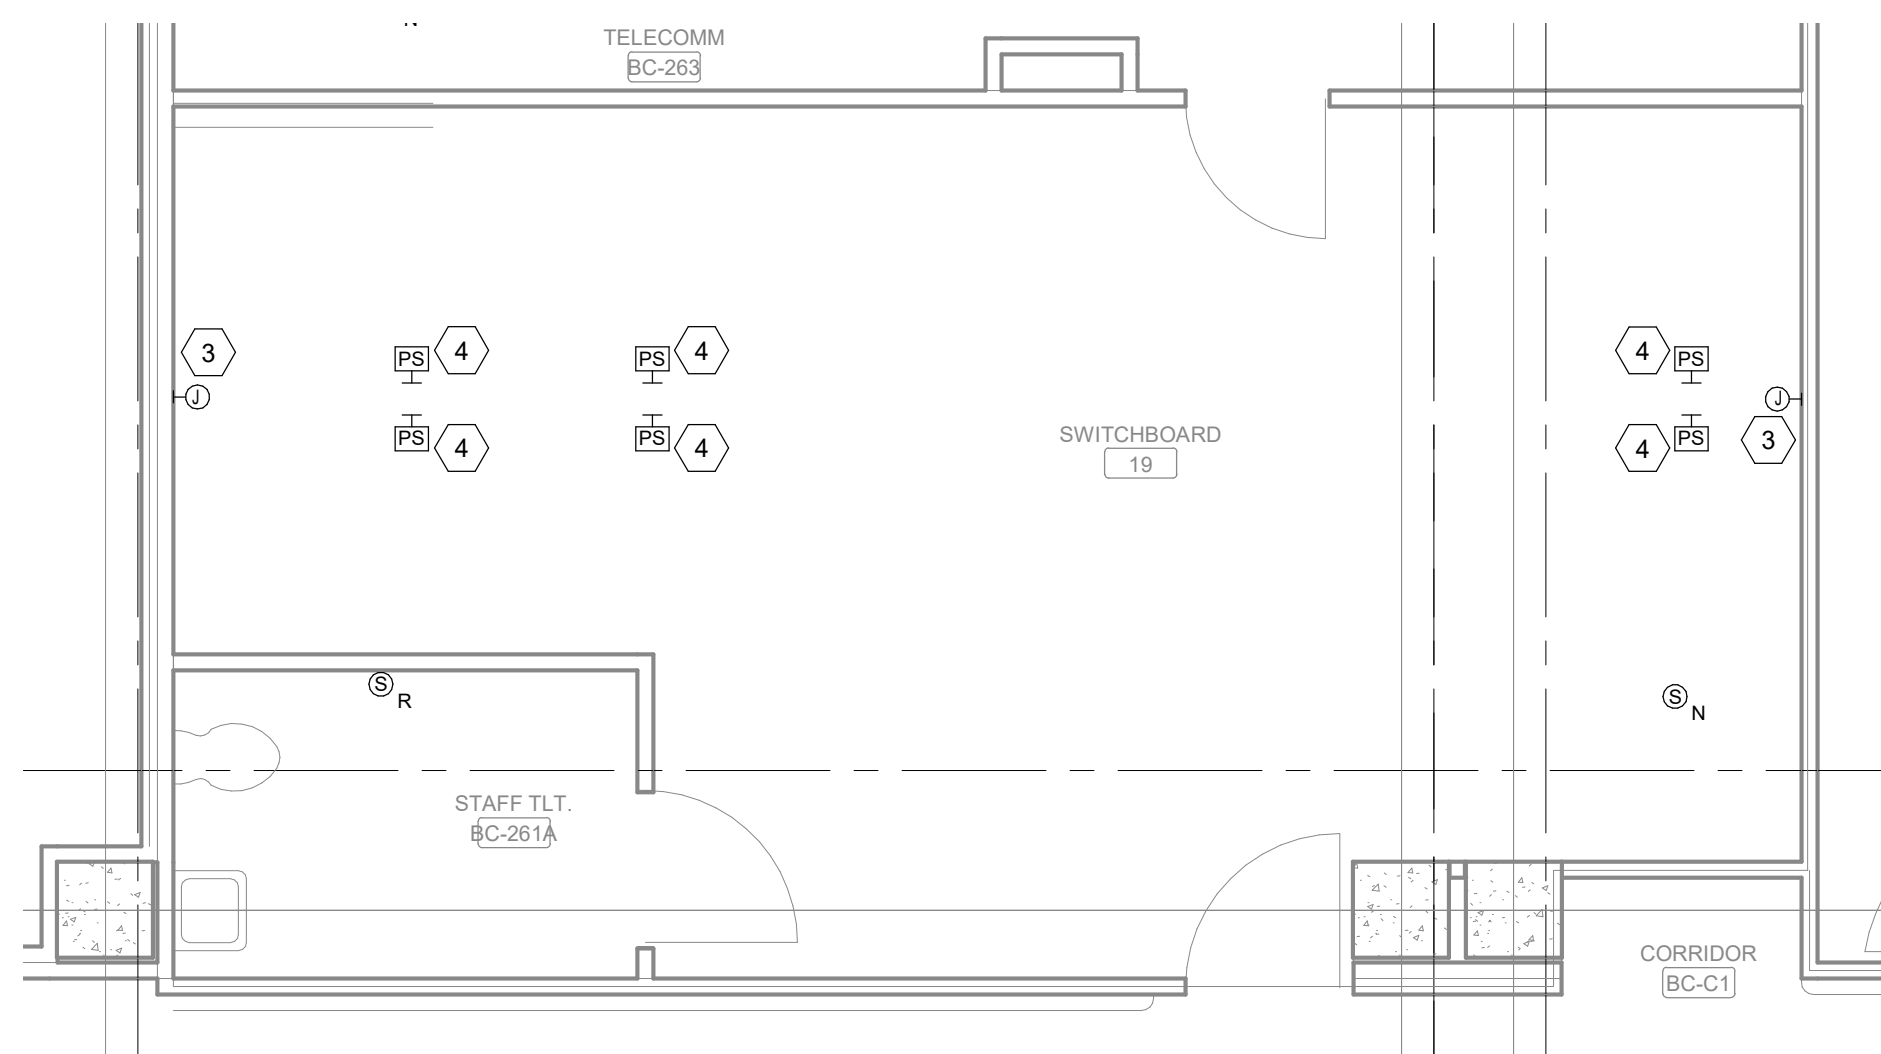

3 BASEMENT ENLARGEMENT - CALL CENTER
Scale: 1/4" = 1'-0"

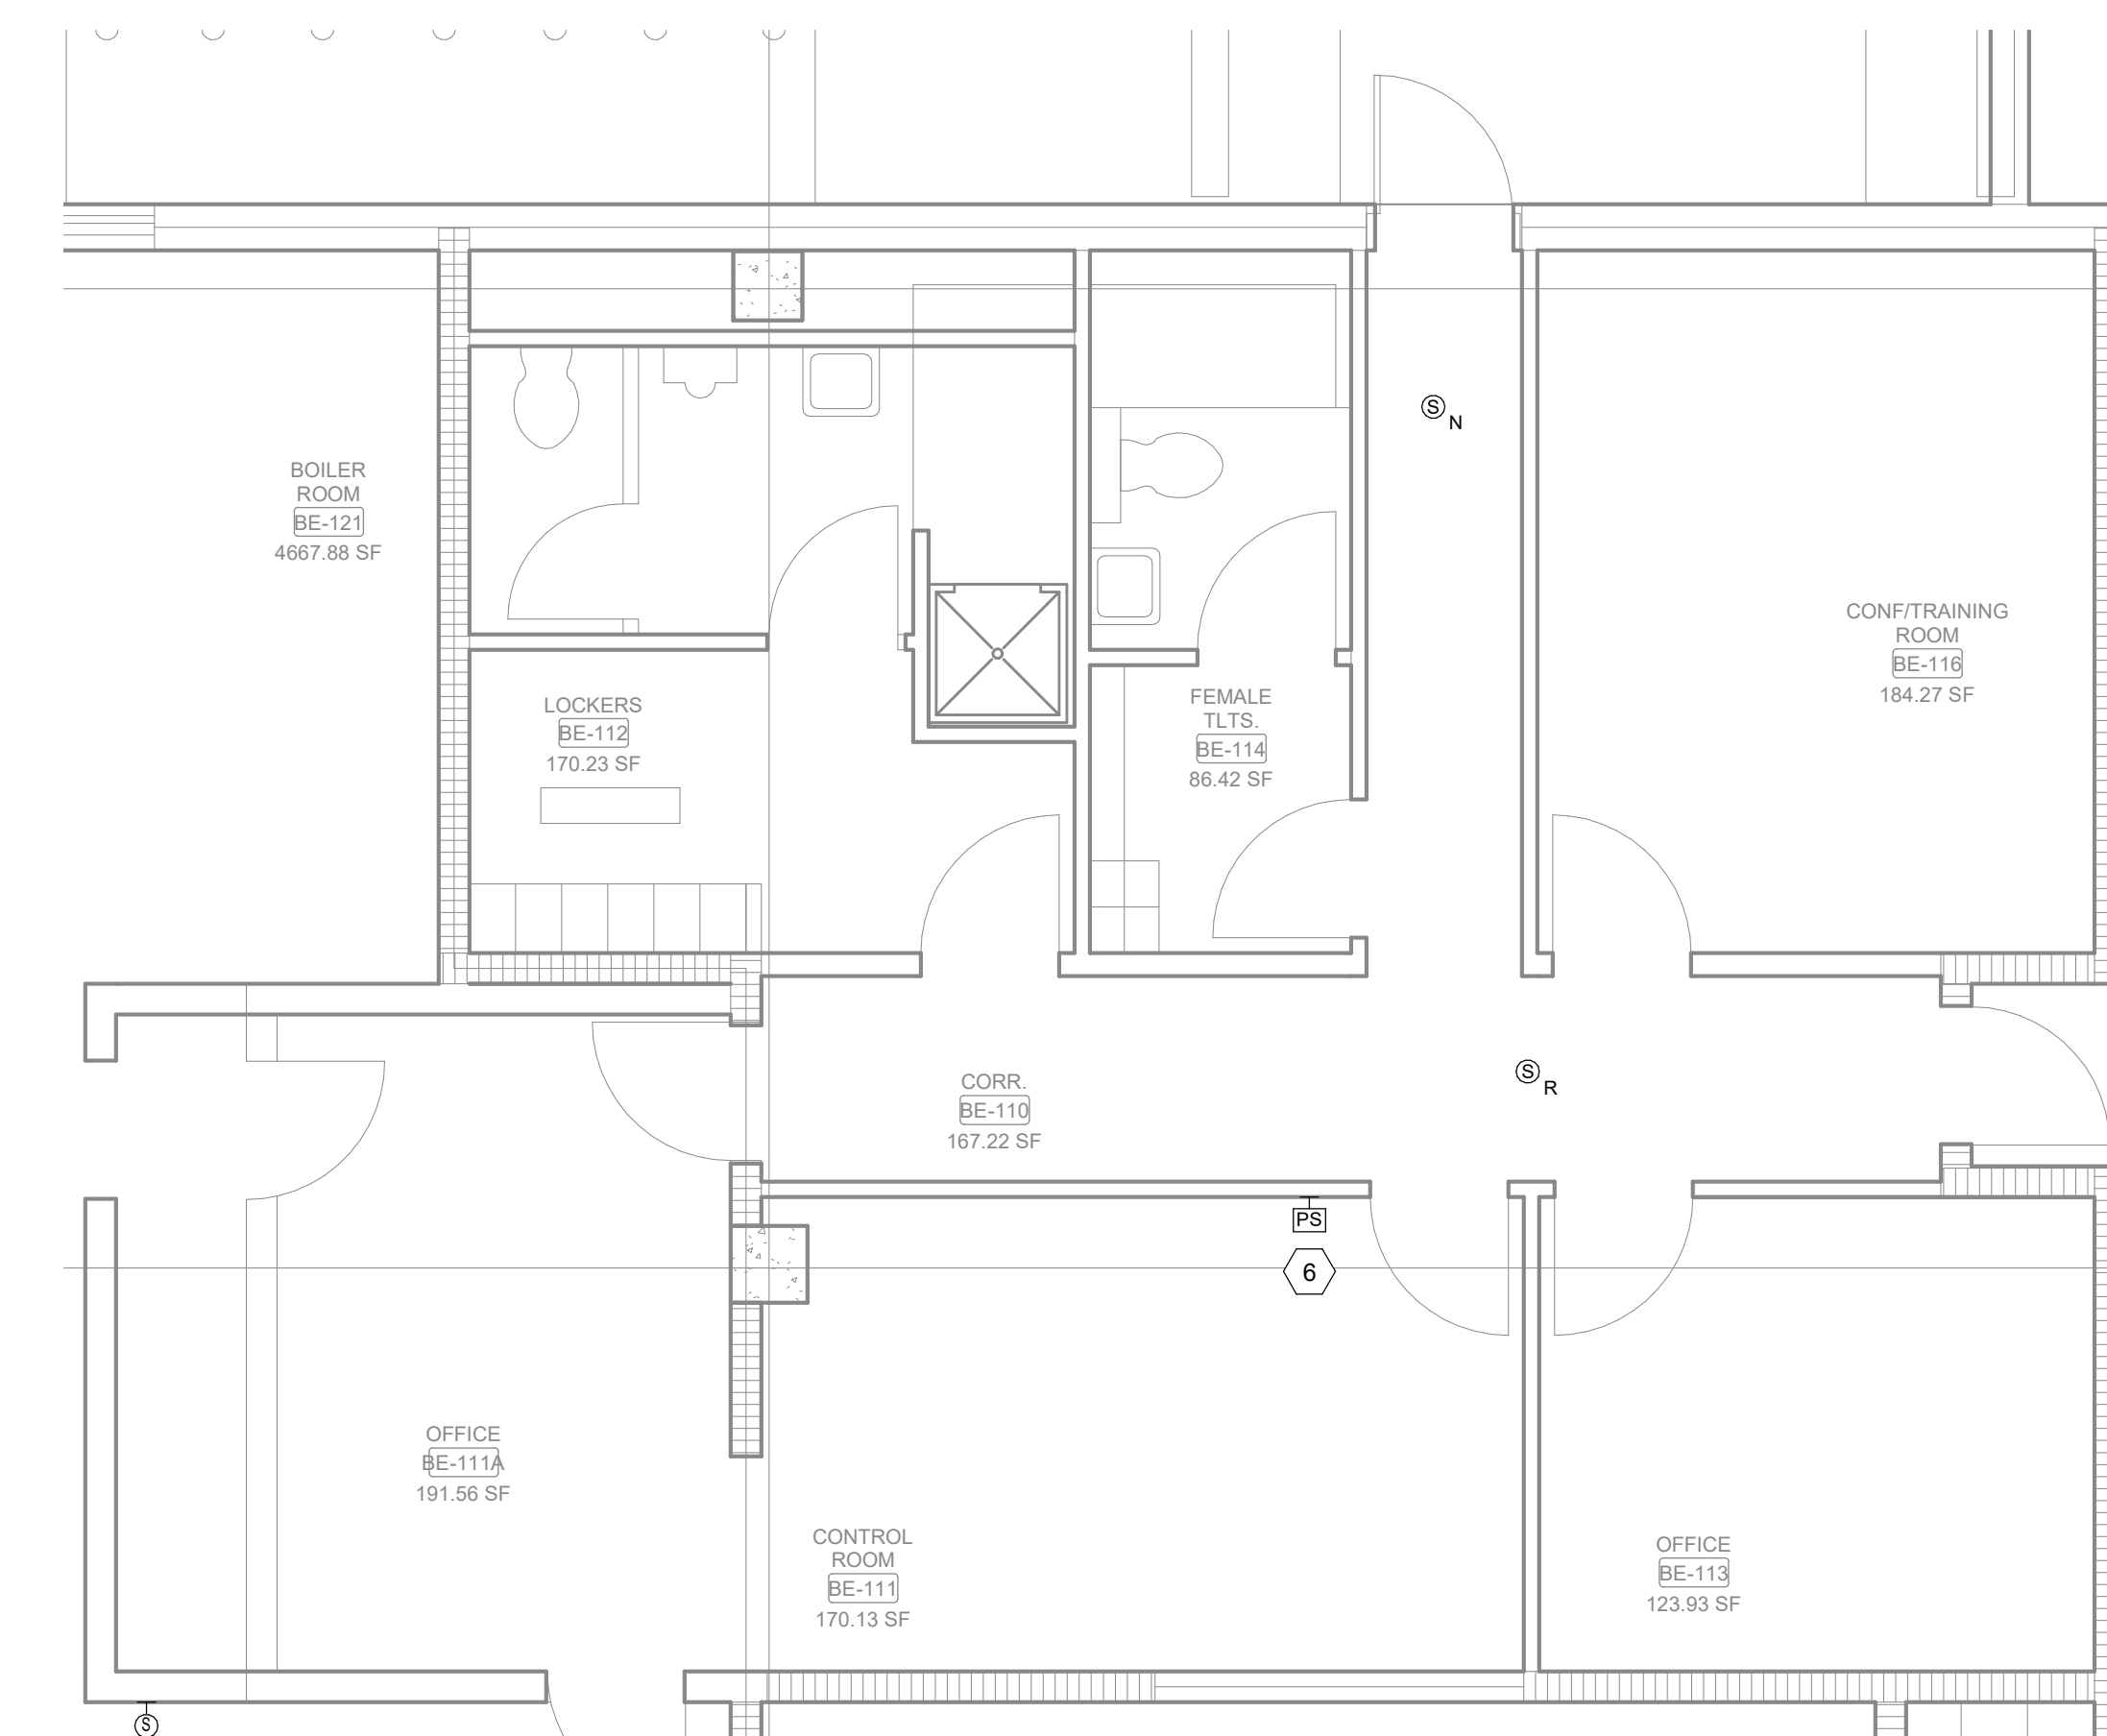

2 BASEMENT ENLARGEMENT - ENERGY CENTER
Scale: 1/4" = 1'-0"

SHEET NOTES:

- A. PROVIDE PAMNS DEVICES AT LOCATIONS INDICATED ON PLANS. PROVIDE WIRING AND CIRCUIT AS INDICATED ON DETAILS.
- B. ALL PAMN WIRING SHALL BE CONCEALED IN WALLS, IN RACEWAY OR AND ABOVE THE CEILING IN CONDUIT.
- C. PAMN WIRING IN UNFINISHED AREAS SHALL BE IN SURFACE MOUNTED RACEWAY (MECH. ROOM, ROOMS WITH NO CEILINGS.)
- D. ALL CEILING SPEAKERS SHALL BE SET AT 1/2 WATT UNLESS NOTED OTHERWISE.
- E. ALL WALL MOUNTED SPEAKERS SHALL BE SET AT 4 WATTS UNLESS NOTED OTHERWISE.
- F. CONTRACTOR RESPONSIBLE FOR PROVIDING AND INSTALLING FIRE SLEEVES FOR FIREWALL. CONTRACTOR SHALL ADEQUATELY REPAIR ANY FIREWALL PENETRATIONS.
- G. WALL MOUNT PAGING STATION BASIS OF DESIGN IS BIAMP WS-10 WALL STATION.
- H. DESK MOUNT PAGING STATION BASIS OF DESIGN IS BIAMP DS-10 DESK STATION.

KEY NOTES:

- 1 VOLUME CONTROL FOR SPEAKERS IN POLICE CENTER.
- 2 VOLUME CONTROL FOR SPEAKERS IN EMERGENCY DEPARTMENT.
- 3 WALL MOUNTED JUNCTION BOX PROVIDING DATA FEED TO PAGING STATIONS. COORDINATE PLACEMENT WITH CASEWORK RACEWAY.
- 4 LOCATION OF DESK MOUNTED DEDICATED PAGING STATION. ROUTE FEED FOR PAGING STATION THROUGH CASEWORK RACEWAY. COORDINATE WITH COR.
- 5 LOCATION OF DESK MOUNTED DEDICATED PAGING STATION. COORDINATE WITH COR.
- 6 LOCATION OF WALL MOUNT DEDICATED PAGING STATION. COORDINATE WITH COR.
- 7 LOCATION OF EXISTING FIRE ALARM CONTROL PANEL. COORDINATE ALL INTERCONNECT WORK WITH COR PRIOR TO PERFORMING WORK.
- 8 LOCATION OF FIRE ALARM INTERFACE PANEL. REFERENCE T-501 DETAIL 2.


WALL RATING LEGEND

- 1 HR - FIRE SEPARATION
- 2 HR - FIRE SEPARATION
- SMOKE RESISTIVE HAZARDOUS AREA


FULLY SPRINKLERED

100% CONSTRUCTION DOCUMENTS


CONSULTANTS:		PROJECT MANAGER		Office of Construction and Facilities Management		Drawing Title		Project Title		VA PROJECT NUMBER	
		ACG Project Number 22-038		1151 Kildaire Farm Road, Suite 120 Cary, North Carolina 27511		TECHNOLOGY ENLARGEMENTS		REMOVE AND REPLACE PUBLIC ADDRESS SYSTEM		548-22-100	
		Headquarters: Apogee Consulting Group, P.A.		www.acg-pa.com		Location		Approved		Building Number	
		919-858-7420		U.S. Department of Veterans Affairs		WEST PALM BEACH VAMC 7305 NORTH MILITARY TRAIL WEST PALM BEACH FL, 33410-6400		Date		#	
								Checked		Drawing Number	
								JDM		T-401	
								Date		Dwg	
								DECEMBER 14, 2022		29 of 32	

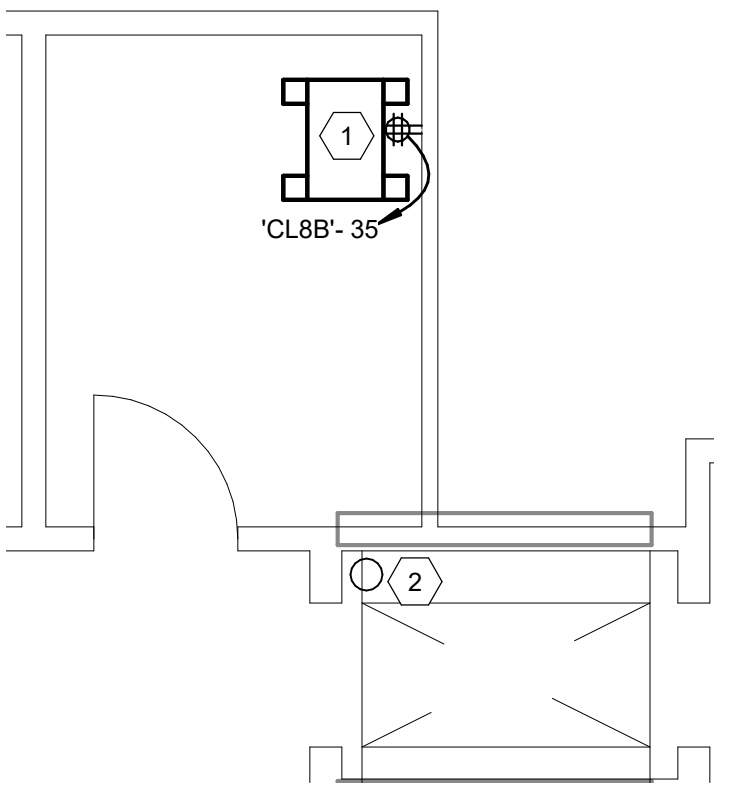


5
HEADEND EQUIPMENT
LOCATION - BUILDING 1
EIGHTH FLOOR 8A-302C
Scale: 1/4" = 1'-0"

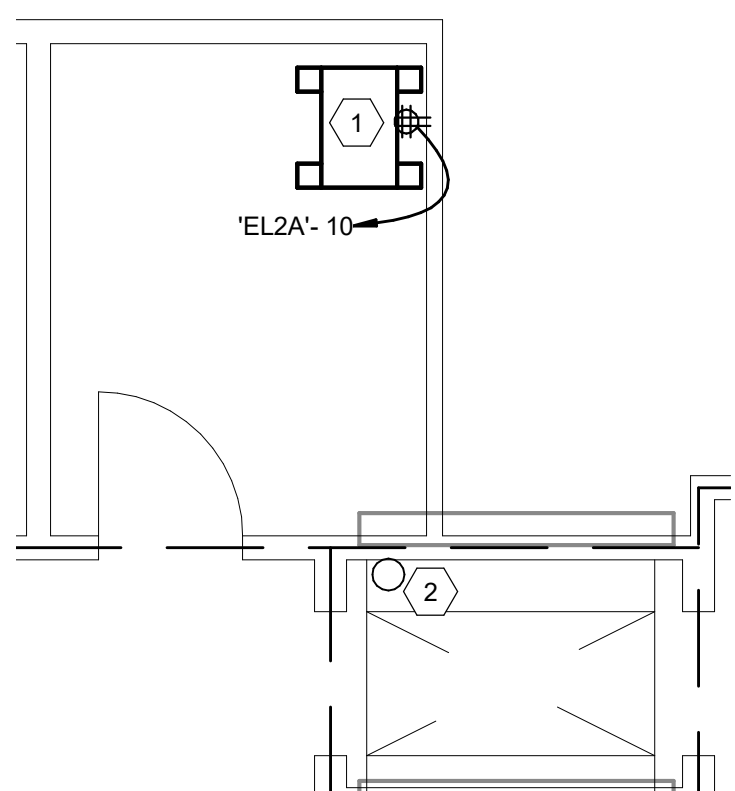


3
HEADEND EQUIPMENT
LOCATION - BUILDING 1
SECOND FLOOR 2B-302C
Scale: 1/4" = 1'-0"

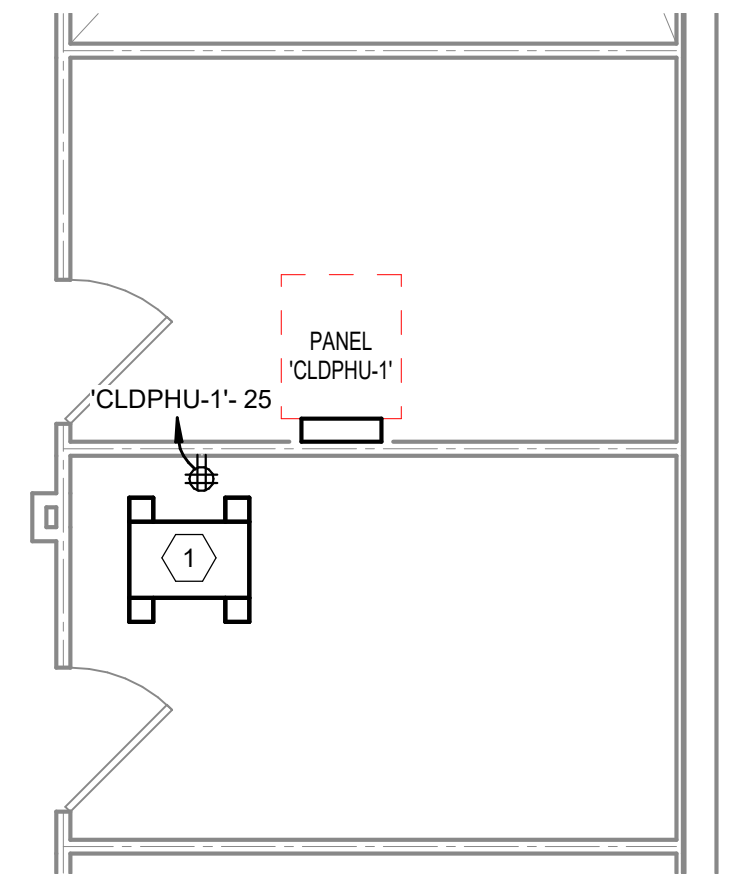

1
HEADEND EQUIPMENT
LOCATION - CLC 1H-103
Scale: 1/4" = 1'-0"

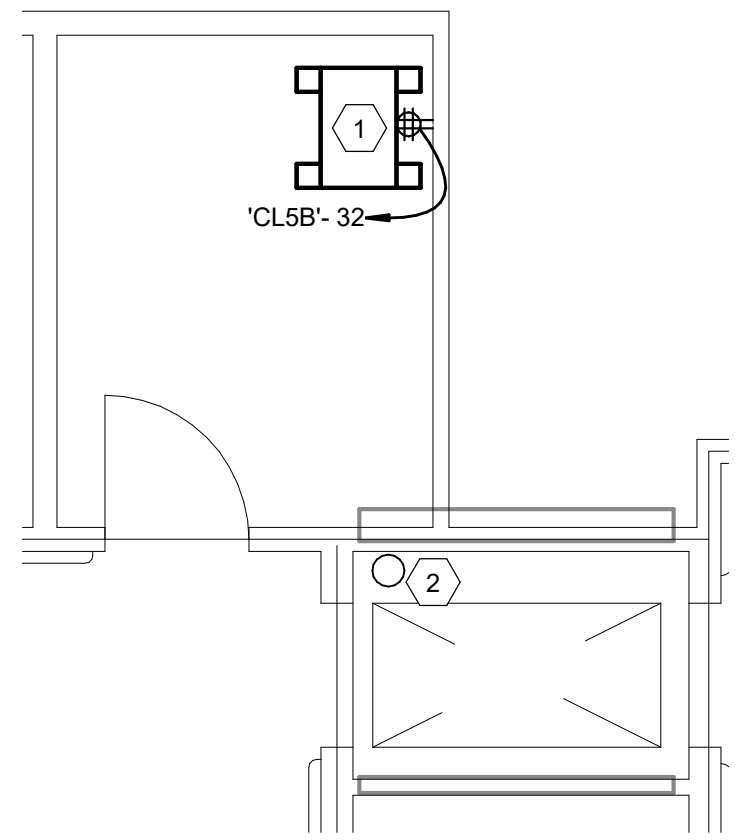

4
HEADEND EQUIPMENT
LOCATION - BUILDING 1
FIFTH FLOOR 5B-302C
Scale: 1/4" = 1'-0"

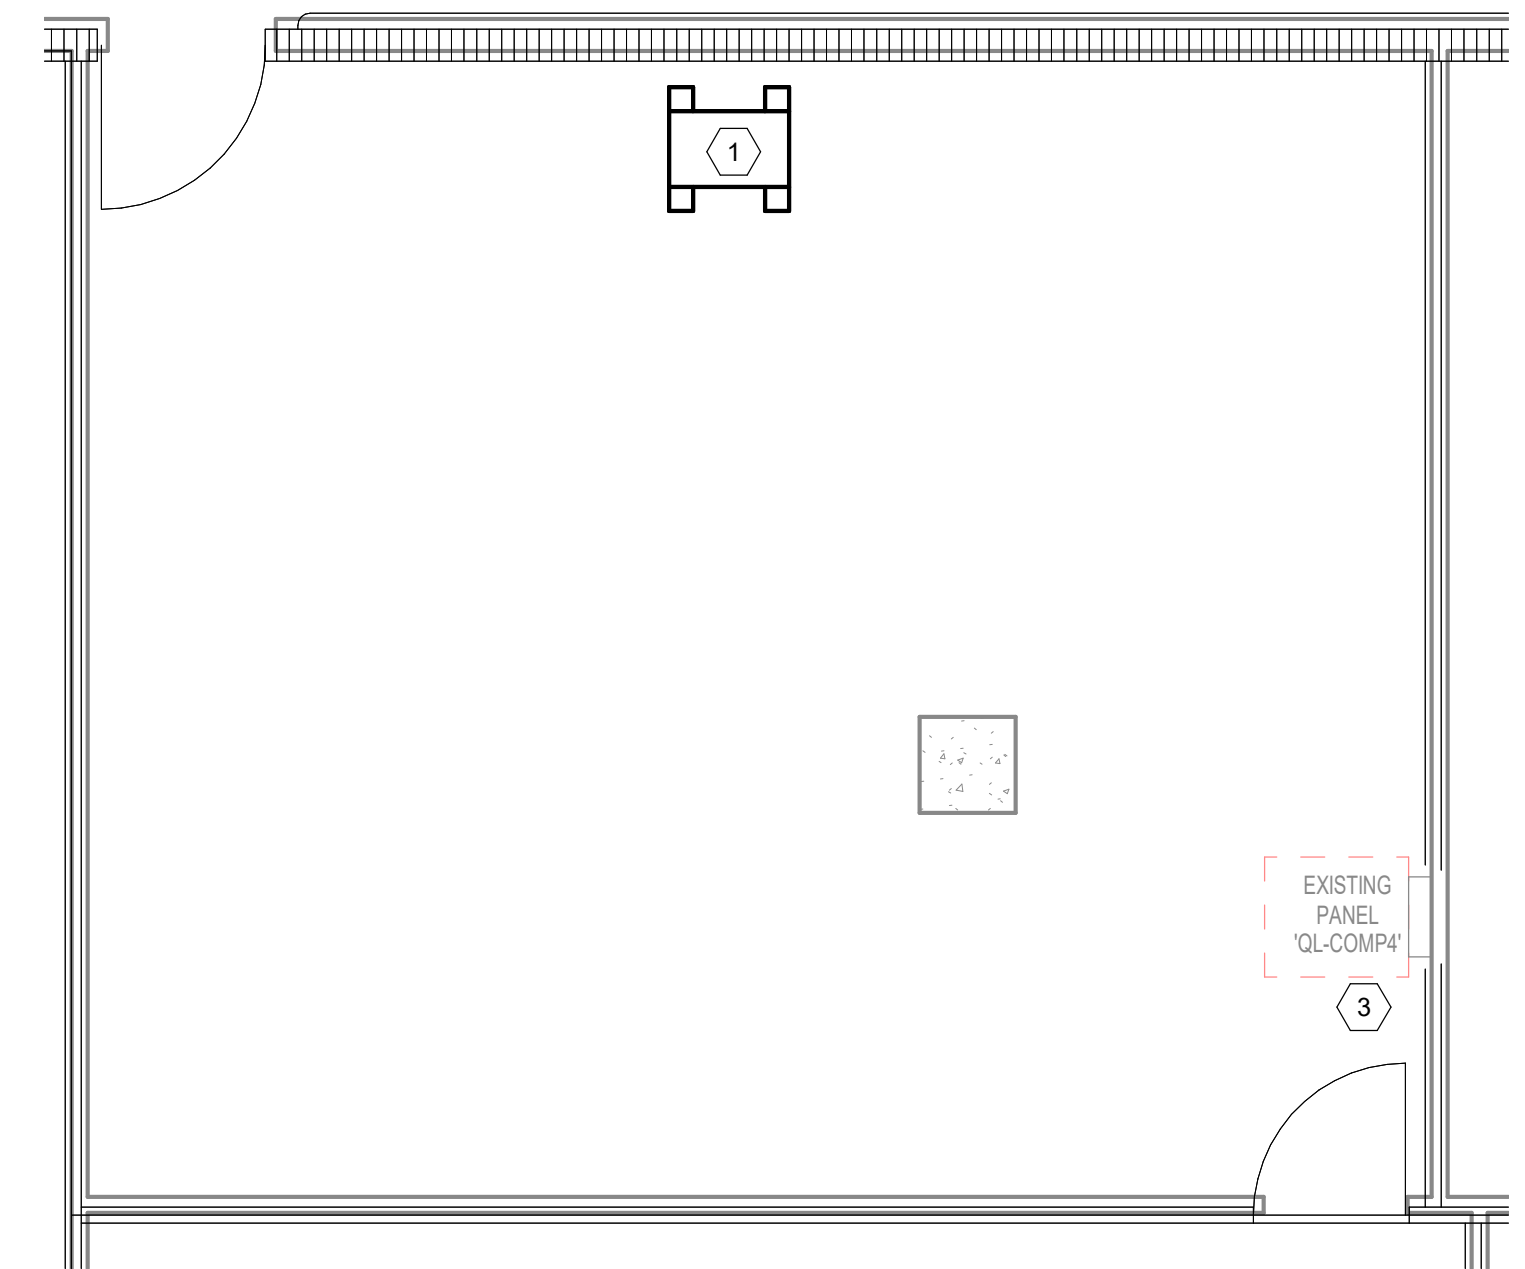

2
HEADEND EQUIPMENT LOCATION - BLDG 1 BASEMENT
BC-202
Scale: 1/4" = 1'-0"

SHEET NOTES:

- PROVIDE PAMNS DEVICES AT LOCATIONS INDICATED ON PLANS. PROVIDE WIRING AND CIRCUIT AS INDICATED ON DETAILS.
- ALL PAMN WIRING SHALL BE CONCEALED IN WALLS, IN RACEWAY OR AND ABOVE THE CEILING IN CONDUIT.
- PAMN WIRING IN UNFINISHED AREAS SHALL BE IN SURFACE MOUNTED RACEWAY (MECH. ROOM, ROOMS WITH NO CEILINGS.)
- CONTRACTOR RESPONSIBLE FOR PROVIDING AND INSTALLING FIRE SLEEVES FOR FIREWALL. CONTRACTOR SHALL ADEQUATELY REPAIR ANY FIREWALL PENETRATIONS.
- ALL RECEPTACLE CONDUCTORS SHALL BE 2-12 AWG, 1-12 AWG EG IN 3/4" CONDUIT MINIMUM UNLESS NOTED OTHERWISE.
- COORDINATE LOCATION OF NEW RECEPTACLES AND DATA CABINETS WITH EXISTING EQUIPMENT LOCATED HEADEND EQUIPMENT LOCATIONS.

#

KEY NOTES:

- NEW PAGING EQUIPMENT LOCATION. REFERENCE SHEET E-601 FOR RACK DEVICE LAYOUT AND E-601 FOR RISER DIAGRAM.
- LOCATION OF VERTICAL RISER IN LIFT SHAFT. REF. T-601.
- EXISTING PANEL FEEDING EQUIPMENT RACK IN BC-202. NO WORK ANTICIPATED. PANEL INDICATED FOR DISCONNECTION AS NEEDED.


WALL RATING LEGEND

- 1 HR - FIRE SEPARATION
- 2 HR - FIRE SEPARATION
- SMOKE RESISTIVE HAZARDOUS AREA


FULLY SPRINKLERED

100% CONSTRUCTION DOCUMENTS



	</
--	--	----

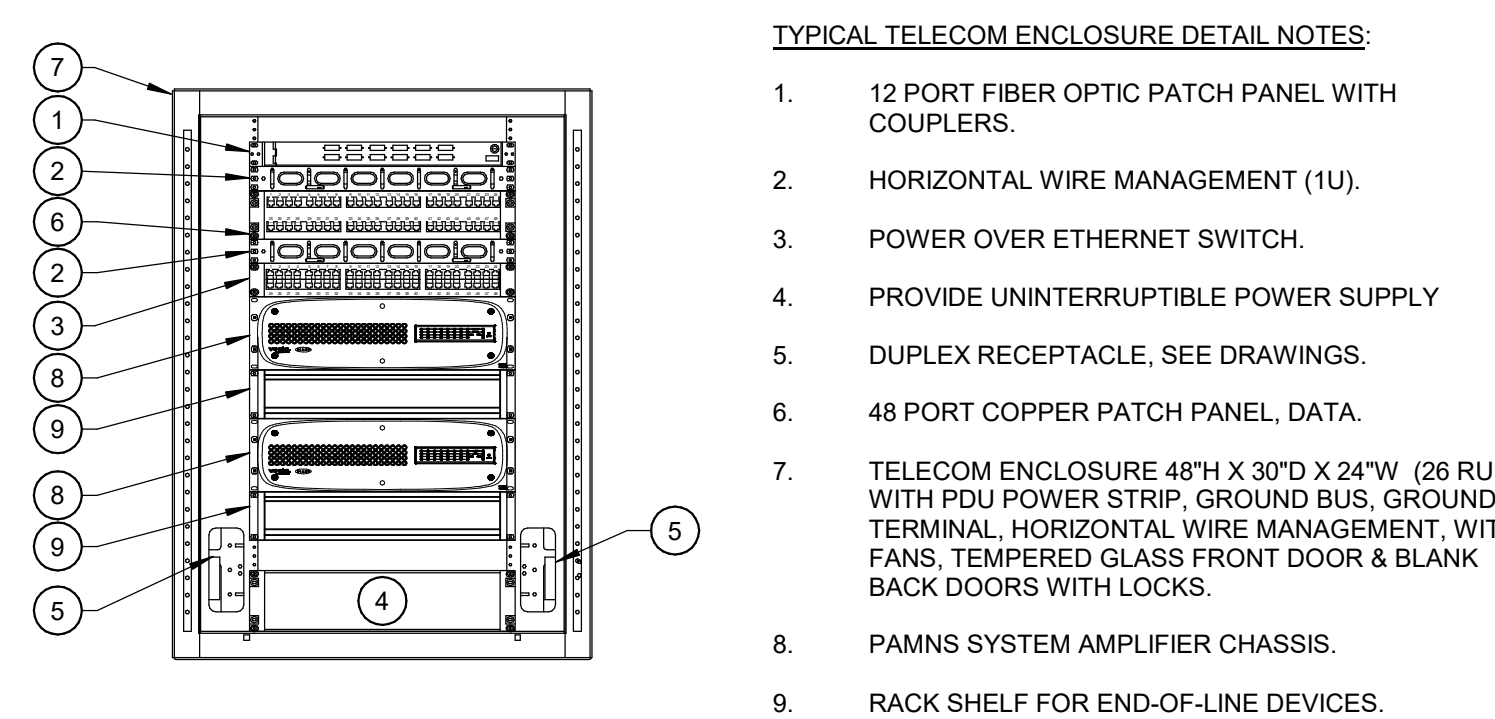


PAMNS HEAD END EQUIPMENT CABINET
TELECOM 2B-302C
TELECOM 5B-302C
TELECOM 8A-302C
Scale: No Scale

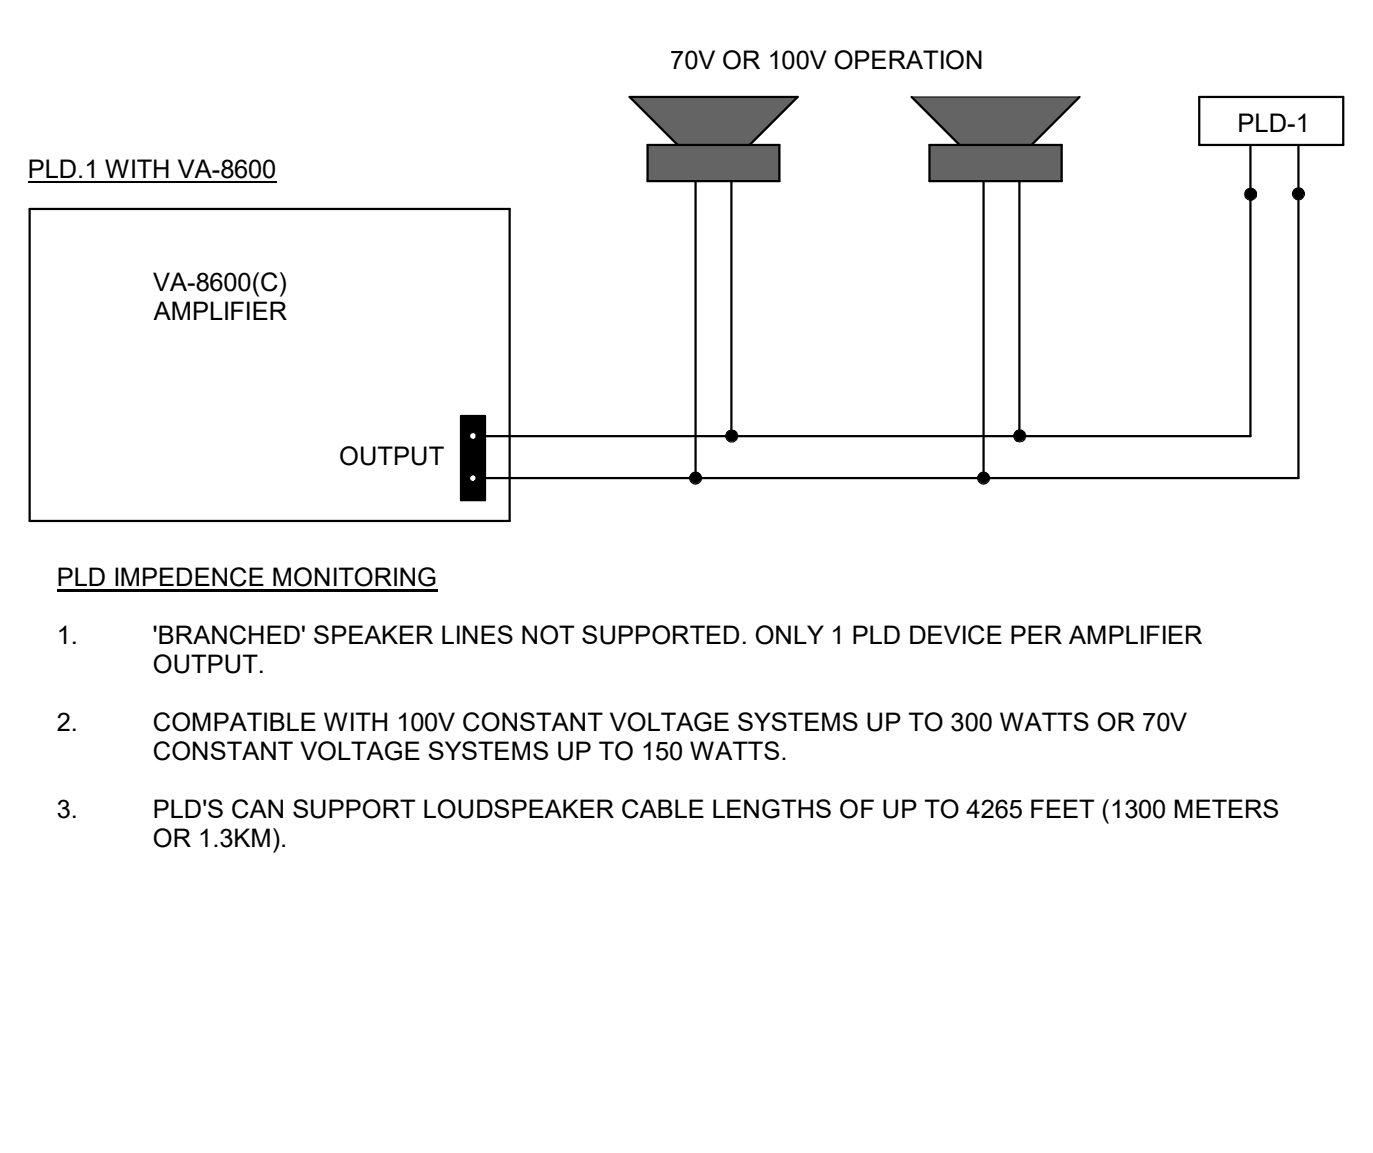


7 LINE MONITORING DEVICE COMPARISON
Scale: No Scale

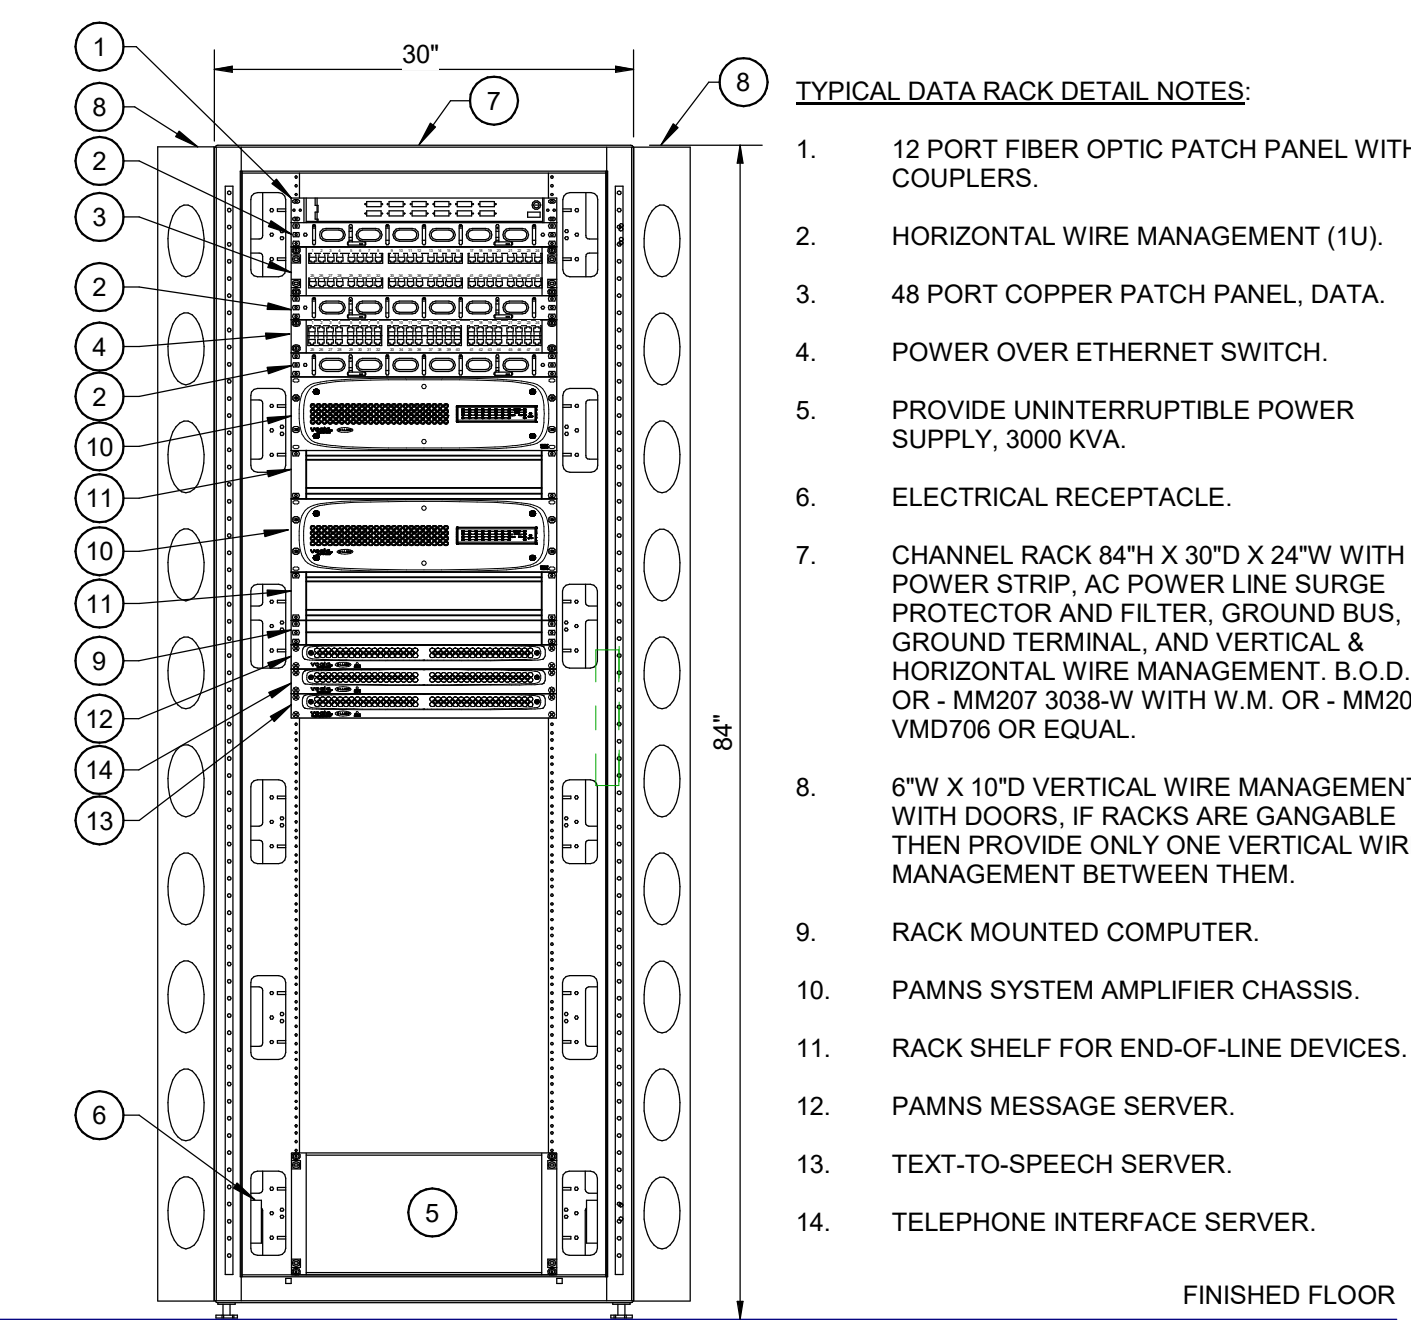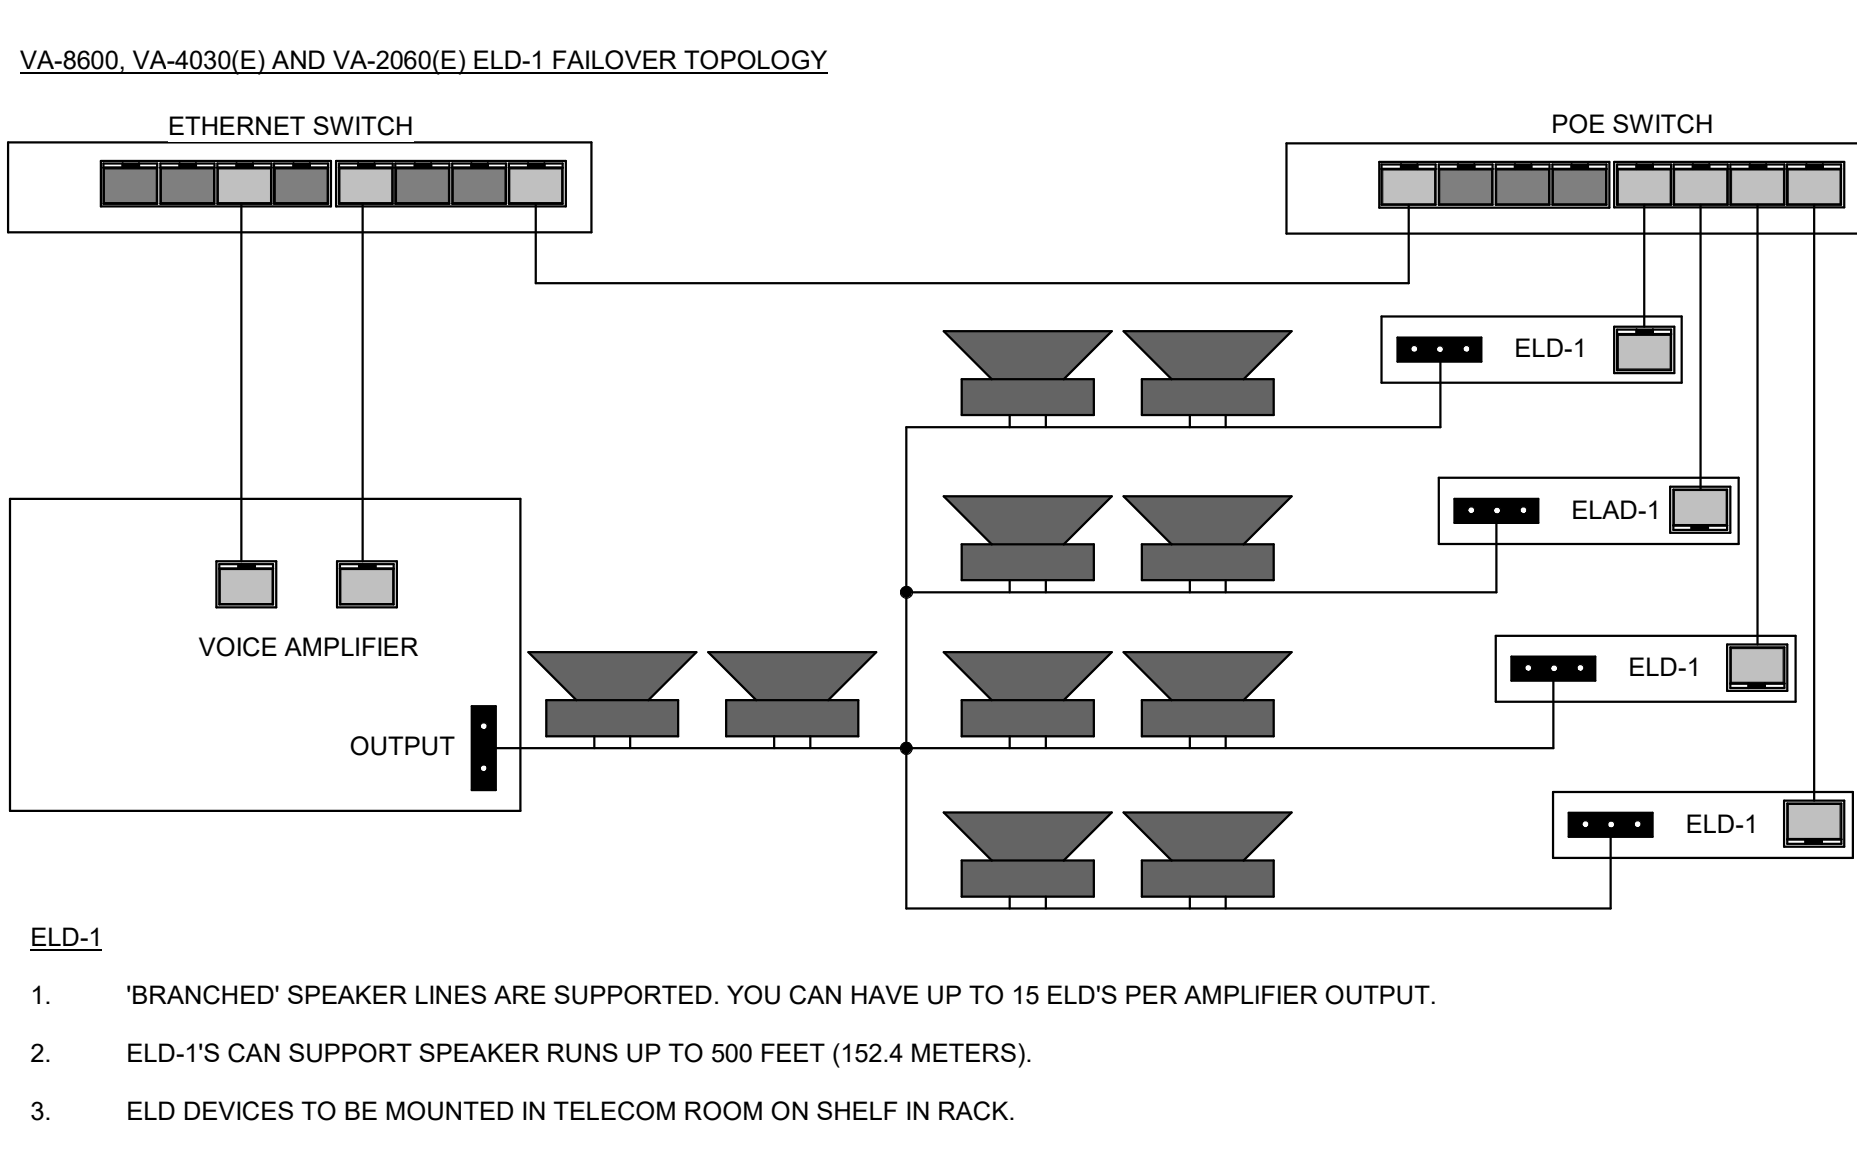


4 PAMNS HEAD END EQUIPMENT RACK
EQUIP. TECH WORK ROOM BC-202
Scale: No Scale

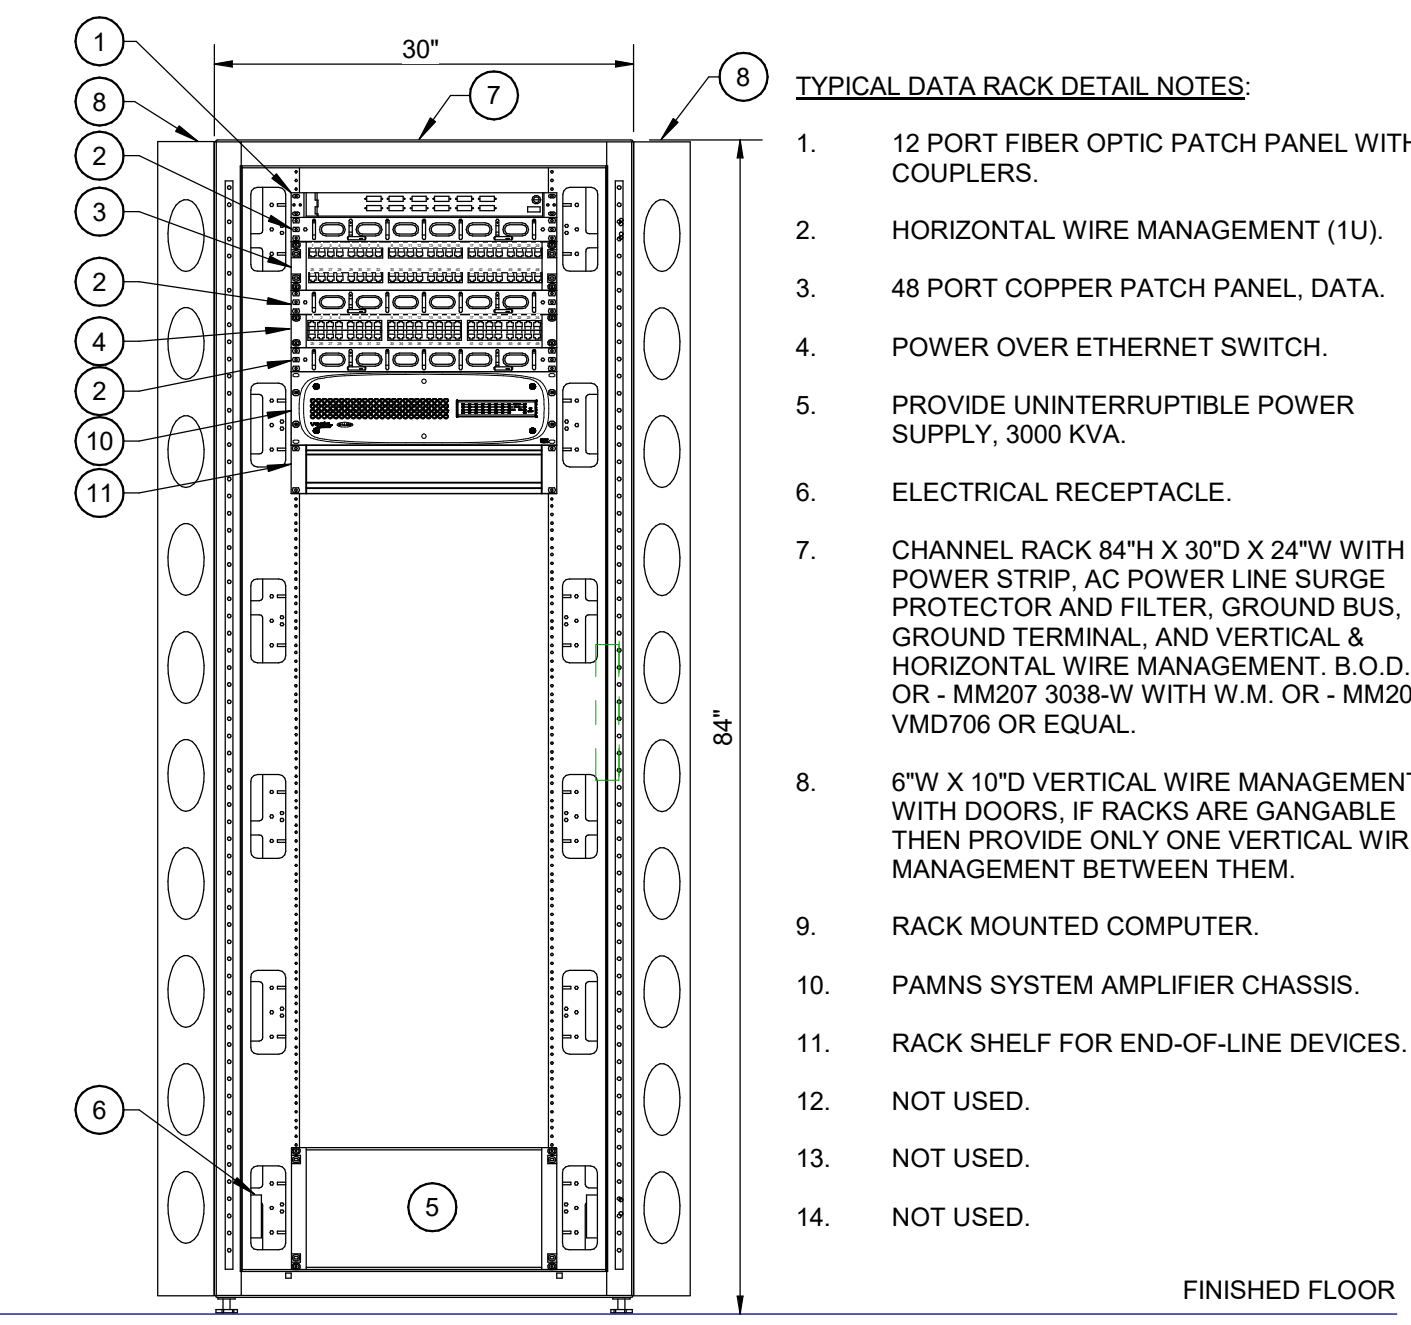


5 PAMNS HEAD END EQUIPMENT RACK
TELECOM 1H-103
Scale: No Scale

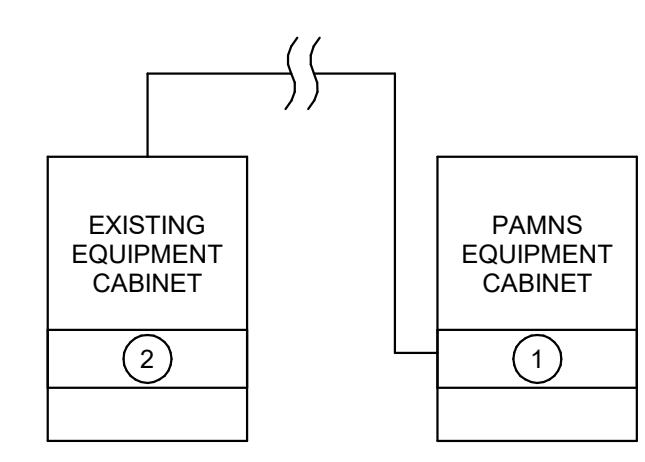

1 PAMNS TELEPHONE INTERFACE
Scale: No Scale

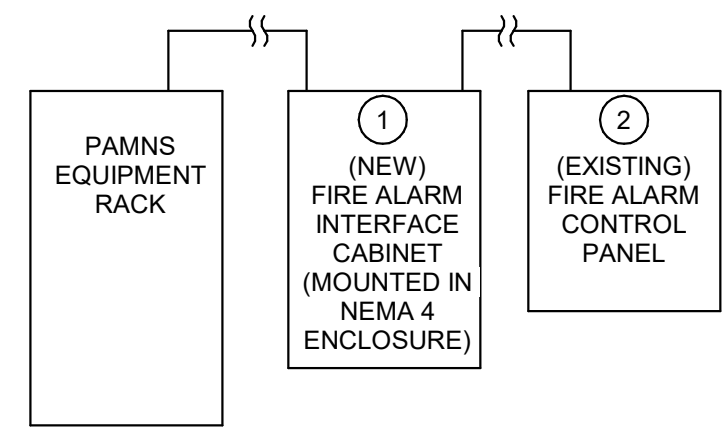

2 PAMNS FIRE ALARM INTERFACE
Scale: No Scale

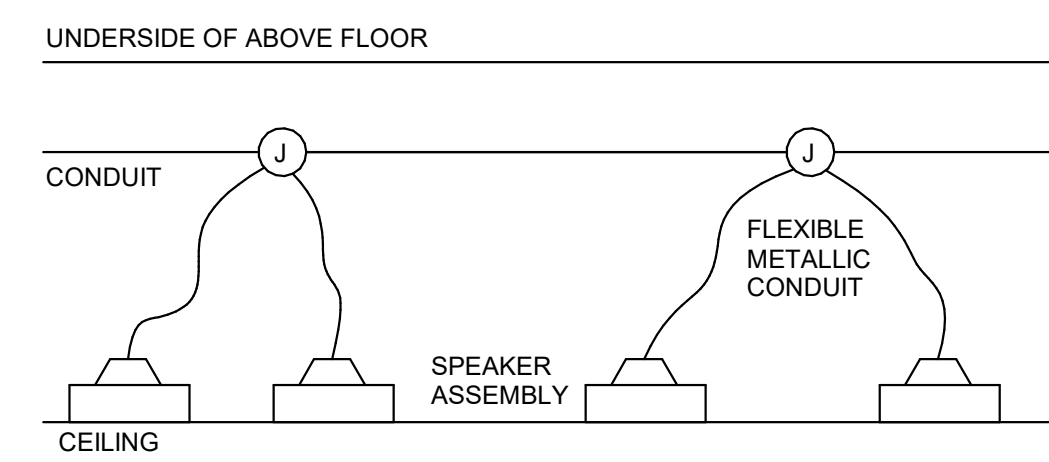

3 SPEAKER CABLING DETAIL
Scale: No Scale

SHEET NOTES:



A. SYSTEM BASIS OF DESIGN DEVICES FOR THE HEAD END EQUIPMENT ARE THE FOLLOWING:

- PAMNS SYSTEM AMPLIFIER CHASSIS: VOCIA VA-8600 AMPLIFIER
- PAMNS SYSTEM AMPLIFIER CARD: AM-800
- PAMNS MESSAGE SERVER: VOCIA MS-1
- TEXT-TO-SPEECH SERVER: VOCIA TTS-1
- TELEPHONE INTERFACE SERVER: VOCIA VOIP-1POTS-1
- FIRE ALARM INTERFACE DEVICE: VOCIA GPIO-1

B. REFERENCE PAMNS RISER DIAGRAM SHEET T-601.

C. CONTRACTOR MAY UTILIZE EITHER PLD OR ELD-1 AS END OF LINE MONITORING DEVICE. CONTRACTOR SHALL MEET THE REQUIREMENTS OF DETAIL 7 THIS SHEET. CONTRACTOR SHALL UTILIZE ELD-1 INSTEAD OF PLD WHERE CONDITIONS PERMIT.

FULLY SPRINKLERED
100% CONSTRUCTION DOCUMENTS

 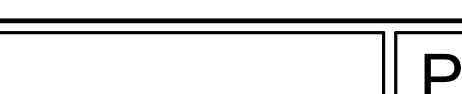			CONSULTANTS:						PROJECT MANAGER		ACG Project Number 22-038		Office of Construction and Facilities Management		Drawing Title TECHNOLOGY DETAILS		Project Title REMOVE AND REPLACE PUBLIC ADDRESS SYSTEM		VA PROJECT NUMBER 548-22-100		
										 Headquarters: Apogee Consulting Group, P.A. 1151 Kildaire Farm Road, Suite 120 Cary, North Carolina 27511		www.acg-pa.com		919-858-7420		Location WEST PALM BEACH VAMC 7305 NORTH MILITARY TRAIL WEST PALM BEACH FL, 33410-6400		Approved		Building Number #	
#	Revisions:	Date								Engineers Architects				VA U.S. Department of Veterans Affairs		Date DECEMBER 14, 2022		Checked JDM		Drawing Number T-501 Dwg 31 of 32	

