


□

□

A

FILE NAME: Y:\OCONUS\MultipleSites\2026_1783264_P1360_IAMF\B_Design\DWG\Sheet\08_ARCH\VP1360_1783264_A105.dwg LAYOUT NAME: A-105 FLOOR PLAN PLOTTED: Monday, April 20, 2026 - 12:28pm USER: paul.c.keller1

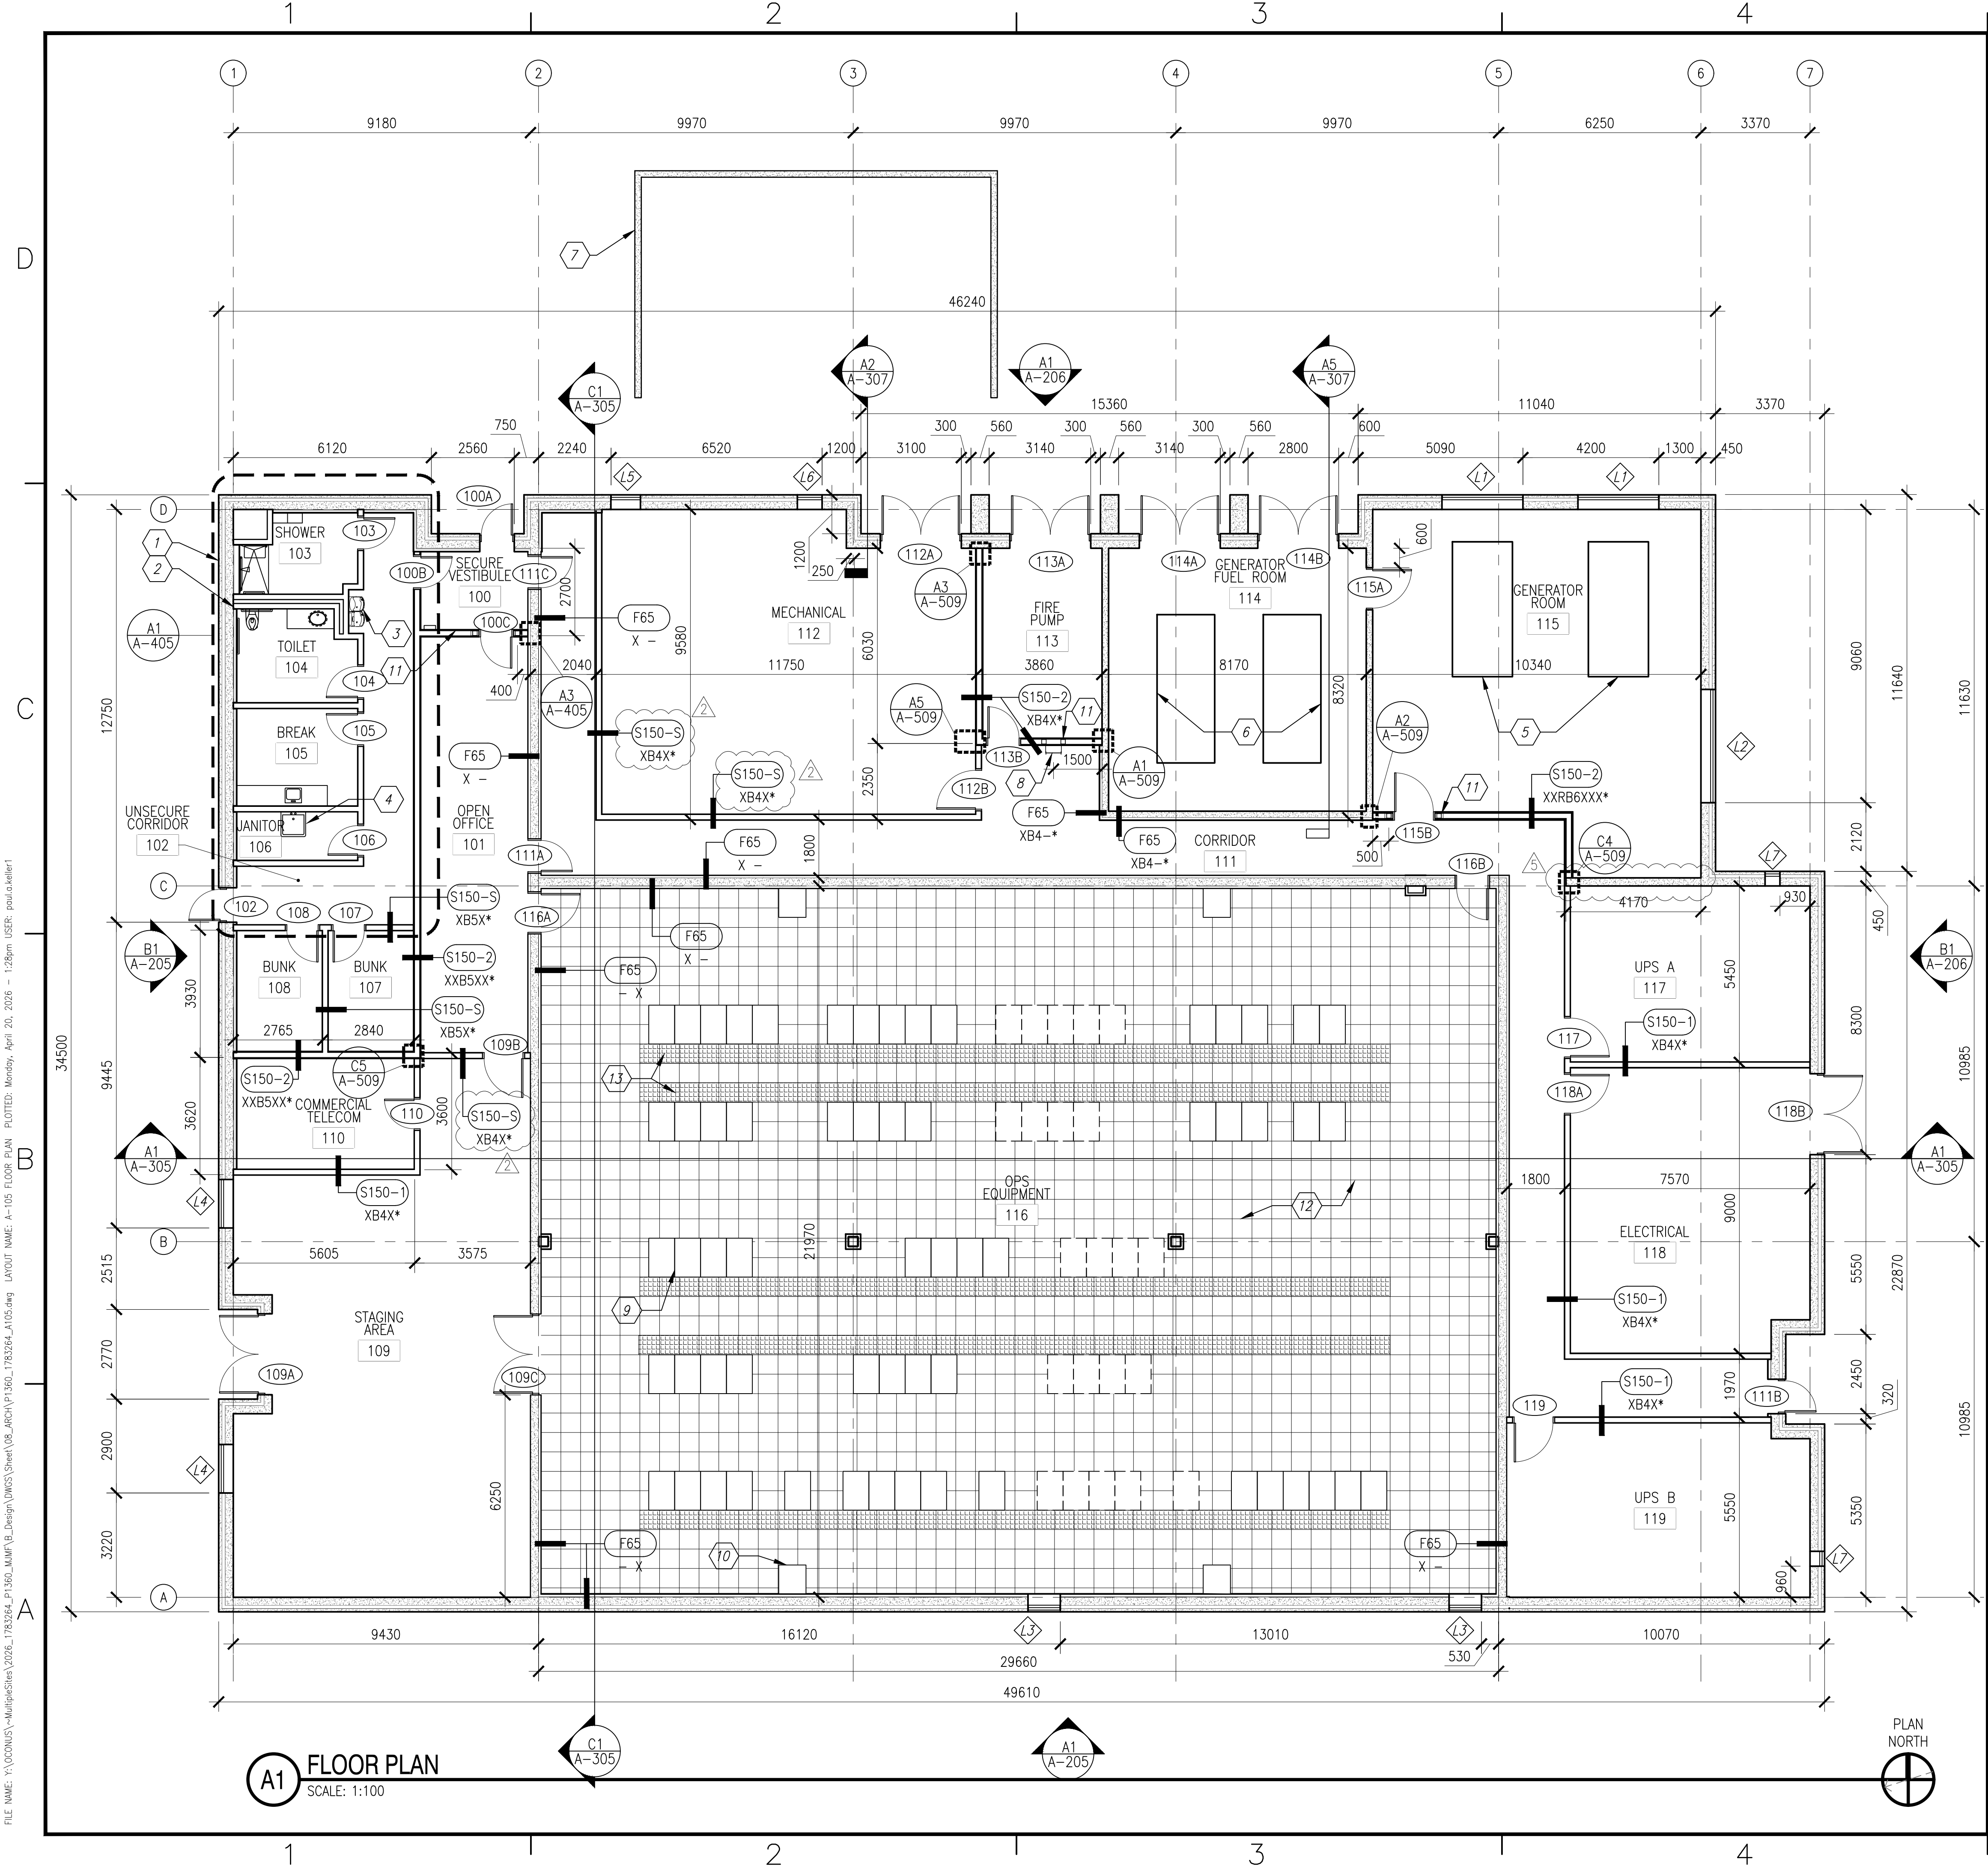

GENERAL SHEET NOTES

A. REFER TO SHEET A-001 FOR ARCHITECTURAL LEGEND AND ABBREVIATIONS.

C. REFER TO SHEET A-101 FOR KEYNOTES THIS SHEET.

D. REFER TO SHEET A-605 FOR PARTITION SCHEDULE.

E. REFER TO SHEET A-606 FOR LOUVER SCHEDULE

F. SEE INTERIOR 'I' SERIES SHEETS FOR FINISH, FURNITURE AND EQUIPMENT LAYOUTS

G. PROVIDE FIRE RETARDANT TREATED WOOD BLOCKING FOR MOUNTING OF GRAB BARS, WALL MOUNTED CABINETS, AV OR IT EQUIPMENT, AND WHERE NECESSARY FOR PROPER ATTACHMENT OF ITEMS. SECURELY ATTACH BLOCKING TO METAL STUD FLANGES. COORDINATE EXACT LOCATION AND QUANTITY OF BLOCKING WITH EQUIPMENT REQUIRING REINFORCEMENT.

H. PROVIDE PLYWOOD BACKBOARDS WHERE REQUIRED FOR COMMUNICATIONS EQUIPMENT. ALL EXPOSED EDGES OF BACKBOARD SHALL BE PAINTED ON FIVE SIDES WITH A FIRE RETARDANT PAINT. SEE ELECTRICAL/TELECOM DRAWINGS FOR ADDITIONAL INFORMATION

I. FINISH FLOOR ELEVATION IS 0.00mm UNLESS OTHERWISE NOTED.

GRAPHIC SCALE

1:100 0 1000 5000 10000mm

NAVAC

DEPARTMENT OF THE NAVY
NAVAL FACILITIES ENGINEERING SYSTEMS COMMAND
PLANNING, DESIGN AND CONSTRUCTION
VARIOUS LOCATIONS

JOINT MARITIME FACILITY
FLOOR PLAN

VARIOUS LOCATIONS

APPROVED

FOR COMMANDER NAVAC

ACTIVITY

D. EVANS VIA EMAIL

SATISFACTORY TO: DATE 01/15/2026

DESIGNER PAK DRAWN PAK CHECKED JHR

PM/DM

BRANCH MANAGER MJD/ATP

DESIGN PROD. DIR. KMC

FIRE PROTECTION ENGINEER WBF DSN

SCALE: AS NOTED

APPROVED NO.: 1838720

CONSTR. CONTR. NO.


NAVAC DRAWING NO. 14157120

SHEET 58 OF 170

A-105

NAVAC METRIC DRAWING REVISION: 01 OCTOBER 2018

FILE NAME: Y:\OCONUS\MultipleSites\2024_1783264_P1362_JAMFAB_Design\DWG\Sheet\08_ARCH\PT1360_1783264_A106.dwg LAYOUT NAME: A-106 REFLECTED CEILING PLAN PLOTTED: Monday, April 20, 2026 - 12:28pm USER: paula.keller1

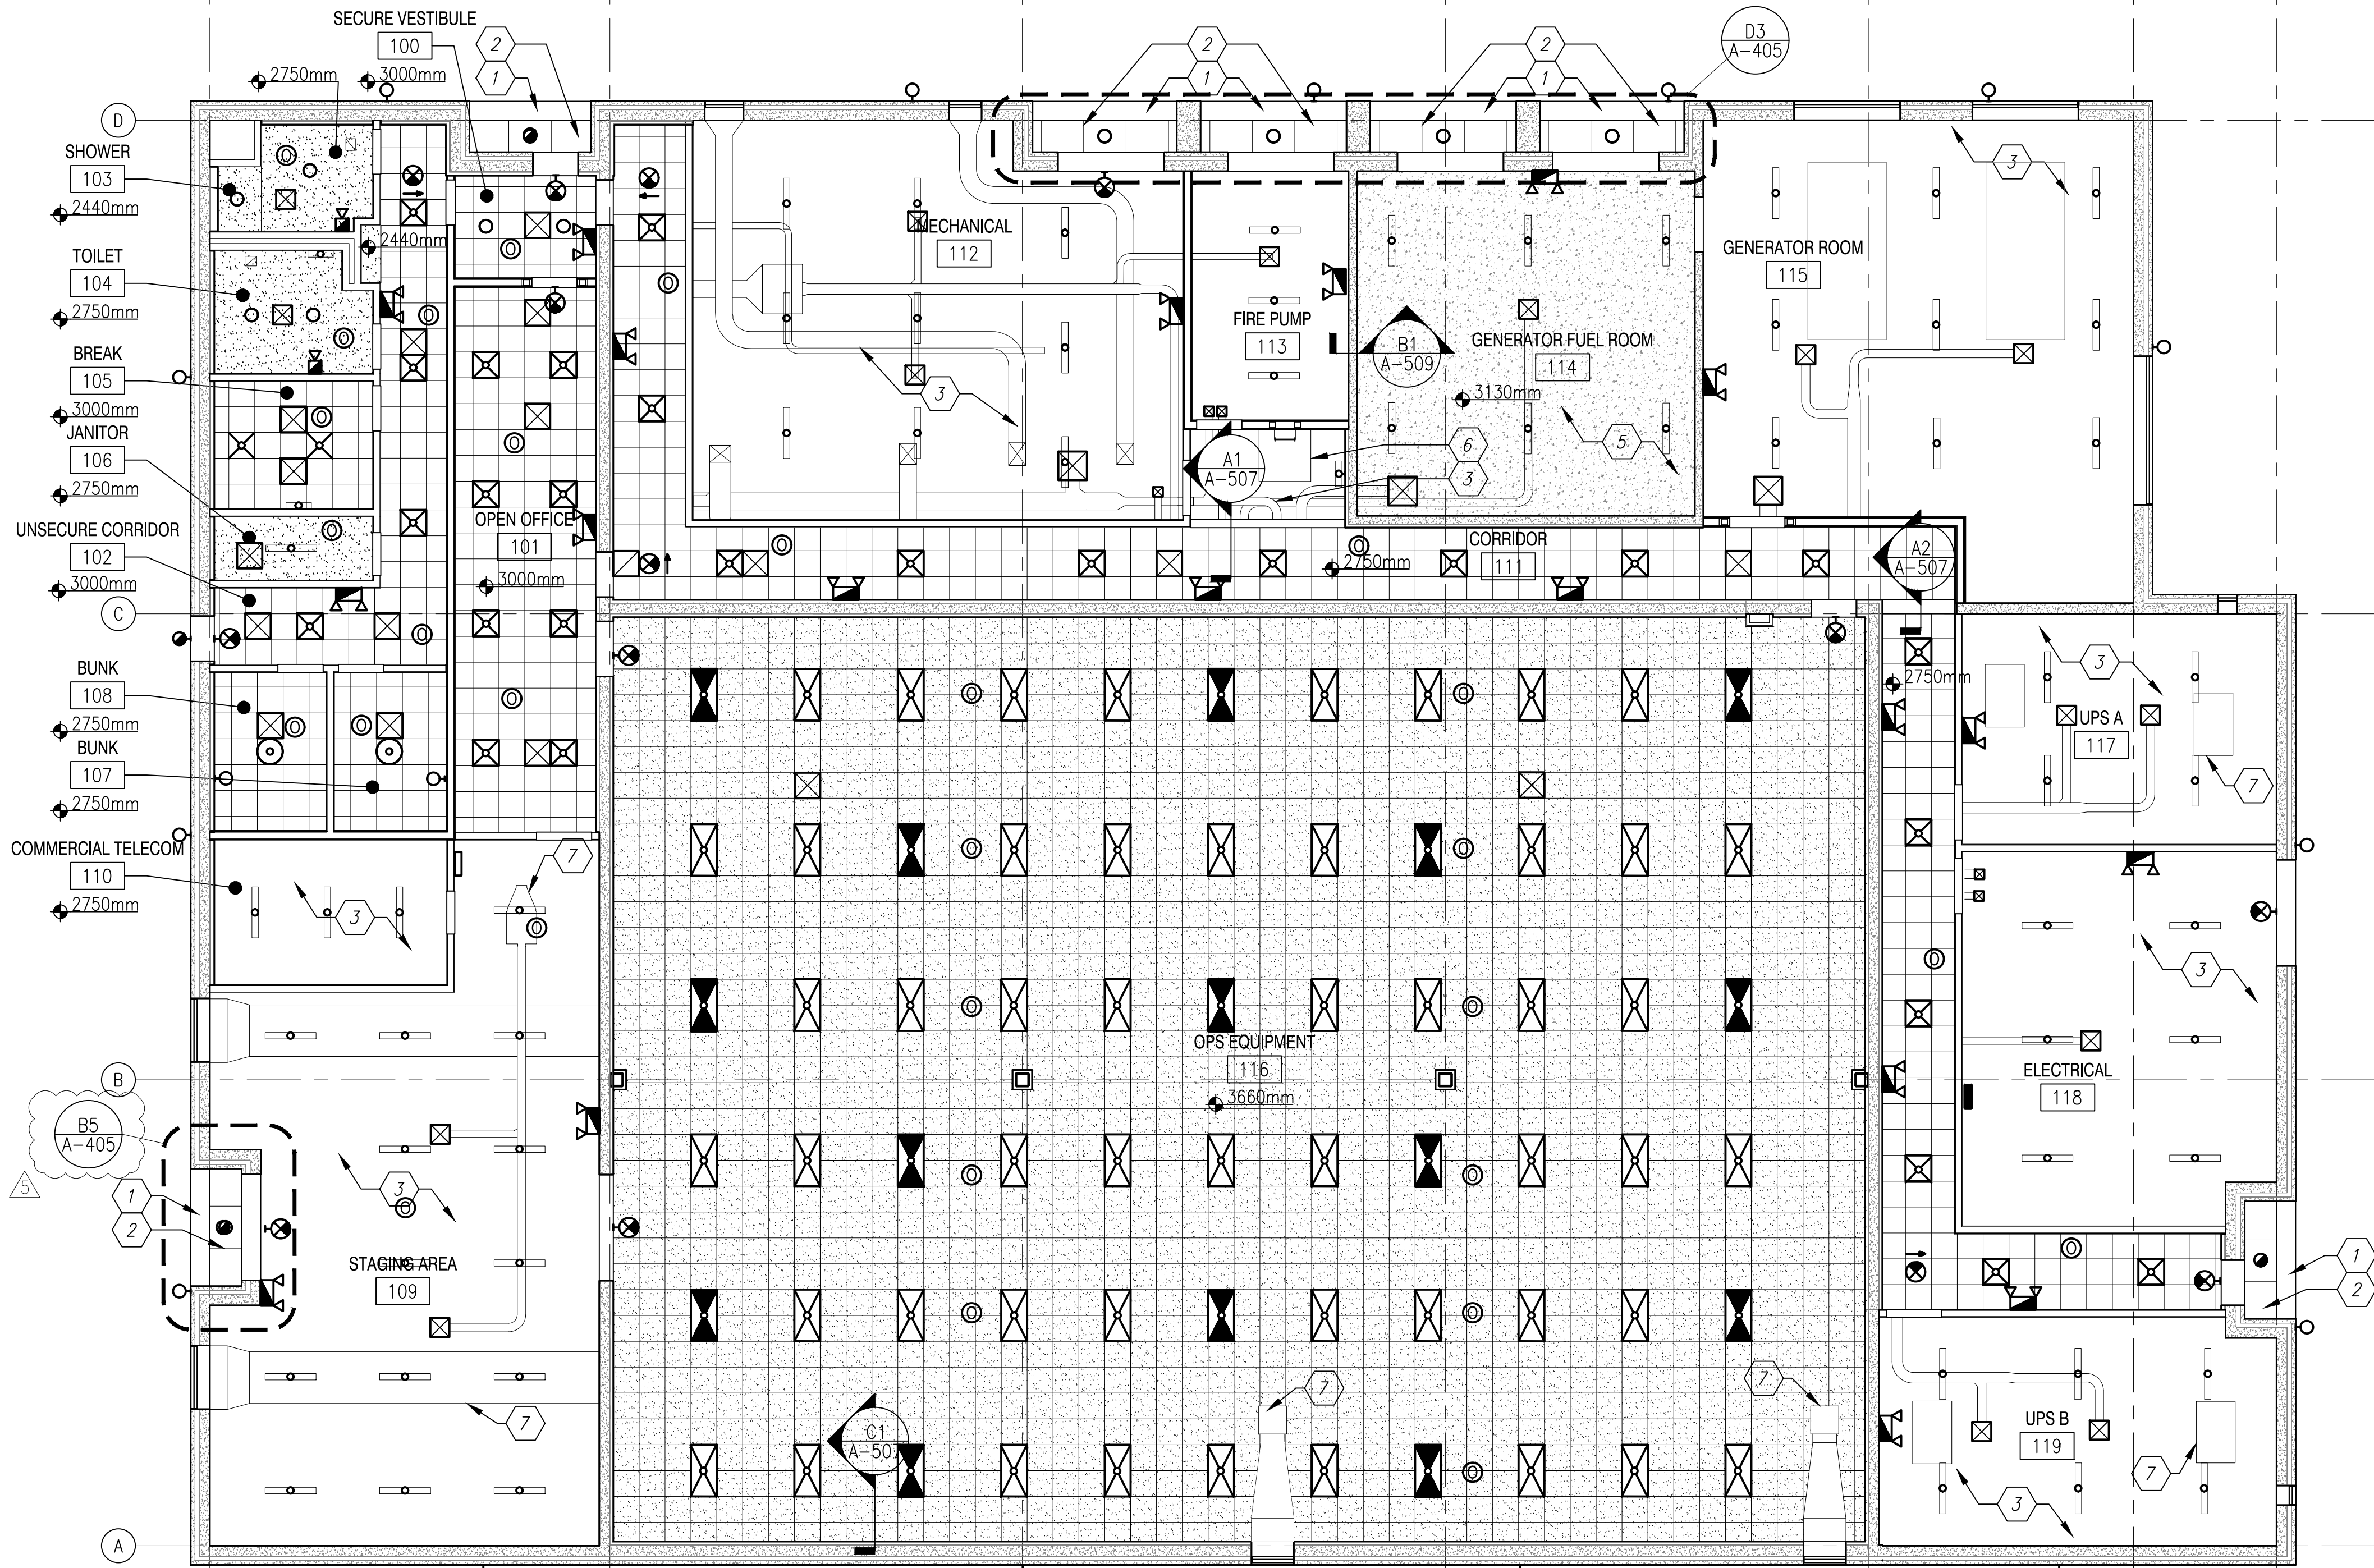

A1 REFLECTED CEILING PLAN
SCALE: 1:100



GENERAL SHEET NOTES

- A. REFER TO SHEET A-001 FOR ARCHITECTURAL LEGEND AND ABBREVIATIONS.
- C. REFER TO SHEET A-101 FOR KEYNOTES THIS SHEET.
- D. REFER TO SHEET A-605 FOR PARTITION SCHEDULE.
- E. REFER TO SHEET A-606 FOR LOUVER SCHEDULE
- F. SEE INTERIOR 'I' SERIES SHEETS FOR FINISH, FURNITURE AND EQUIPMENT LAYOUTS
- G. PROVIDE FIRE RETARDANT TREATED WOOD BLOCKING FOR MOUNTING OF GRAB BARS, WALL MOUNTED CABINETS, AV OR IT EQUIPMENT, AND WHERE NECESSARY FOR PROPER ATTACHMENT OF ITEMS. SECURELY ATTACH BLOCKING TO METAL STUD FLANGES. COORDINATE EXACT LOCATION AND QUANTITY OF BLOCKING WITH EQUIPMENT REQUIRING REINFORCEMENT.
- H. PROVIDE PLYWOOD BACKBOARDS WHERE REQUIRED FOR COMMUNICATIONS EQUIPMENT. ALL EXPOSED EDGES OF BACKBOARD SHALL BE PAINTED ON FIVE SIDES WITH A FIRE RETARDANT PAINT. SEE ELECTRICAL/TELECOM DRAWINGS FOR ADDITIONAL INFORMATION
- I. FINISH FLOOR ELEVATION IS 0.00mm UNLESS OTHERWISE NOTED.

REFLECTED CEILING PLAN LEGEND

- 150mm x 1200mm LIGHT FIXTURE - SEE ELECTRICAL DRAWINGS
- 150mm x 600mm LIGHT FIXTURE - SEE ELECTRICAL DRAWINGS
- RECESSED CAN LIGHT - SEE ELECTRICAL DRAWINGS
- WALL MOUNTED EXTERIOR LIGHT - SEE ELECTRICAL DRAWINGS
- OCCUPANCY SENSOR - SEE ELECTRICAL DRAWINGS
- 610mm x 610mm LIGHT FIXTURE - SEE ELECTRICAL DRAWINGS
- 610mm x 1220mm LIGHT FIXTURE - SEE ELECTRICAL DRAWINGS
- ROUND CEILING SURFACE MOUNTED LIGHT FIXTURE - SEE ELECTRICAL DRAWINGS
- RETURN DIFFUSER - SEE MECHANICAL DRAWINGS
- SUPPLY DIFFUSER - SEE MECHANICAL DRAWINGS
- MOISTURE RESISTANT GYPSUM BOARD
- 3HR RATED CEILING: PRECAST CONCRETE ON FIRE PROOFED STEEL BEAMS.
- 610mm X 610mm ACOUSTICAL CEILING PANEL SUSPENDED FROM SUSPENDED GYPSUM WALL BOARD CEILING SYSTEM.
- 610mm X 610mm ACOUSTICAL CEILING PANEL
- SURFACE MOUNTED DOUBLE FACE EXIT SIGNS - SEE ELECTRICAL DRAWINGS
- LED WALL PACKS - SEE ELECTRICAL DRAWINGS

GRAPHIC SCALE





DATE		04/21/26
SYN		DETAIL CALLOUT ADDED
APPR		
SEAL		
A/E INFO		
APPROVED		
FOR COMMANDER NAVFAC		
ACTIVITY		D. EVANS VIA EMAIL
SATISFACTORY TO:	DATE	01/15/2026
DES PAK	DRW	PAK
PM/DM	CHG	JHR
BRANCH MANAGER	MJD/ATP	
DES PROD DIR	KMC	
FIRE PROTECTION ENGINEER	WBF	
VARIOUS LOCATIONS		DSN
NAVAL FACILITIES ENGINEERING SYSTEMS COMMAND		
NAVAL FACILITIES ENGINEERING SYSTEMS COMMAND - ATLANTIC		
PLANNING, DESIGN AND CONSTRUCTION		
VARIOUS LOCATIONS		
JOINT MARITIME FACILITY		
REFLECTED CEILING PLAN		
SCALE:		AS NOTED
APPROVED NO.:		1838720
CONSTR. CONTR. NO.:		
NAVFAC DRAWING NO.:		14157121
SHEET		59 OF 170
A-106		

FILE NAME: Y:\CONUS\MultipleSites\2026_1783264_P1360_JAMF\B_Design\DWG\Sheet\08_ARCH\PT1360_1783264_2026.dwg LAYOUT NAME: A-205 ELEVATIONS PLOTTED: Monday, April 20, 2026 - 13:26m USER: paulakeller1

B1 NORTH ELEVATION
SCALE: 1:100

A1 WEST ELEVATION
SCALE: 1:100

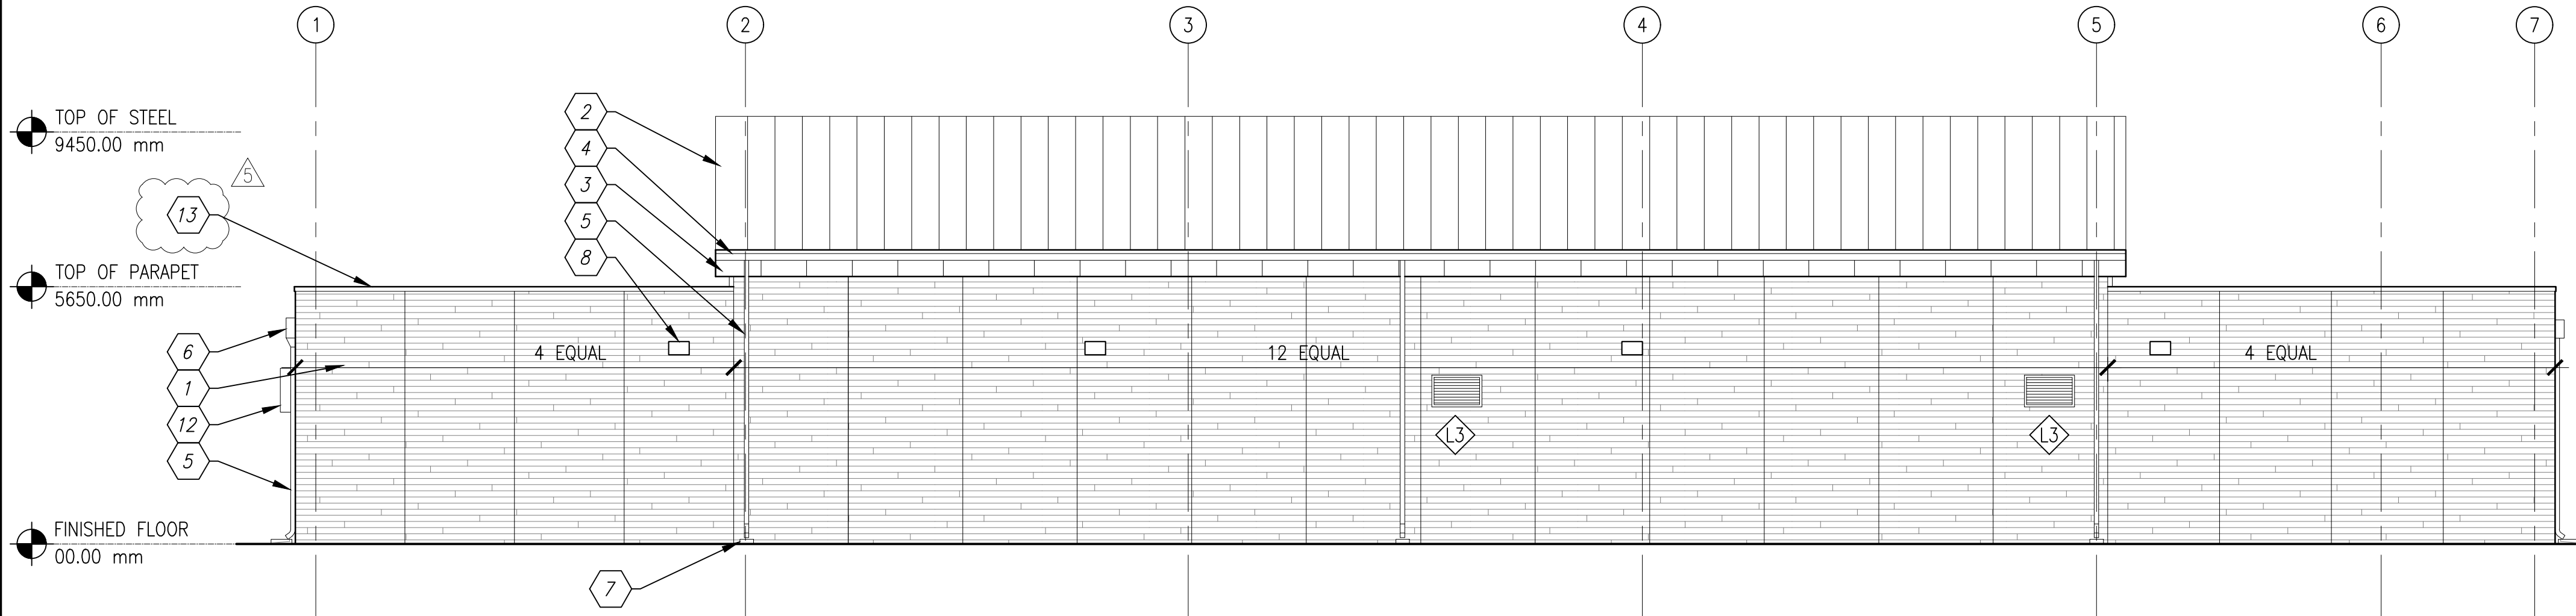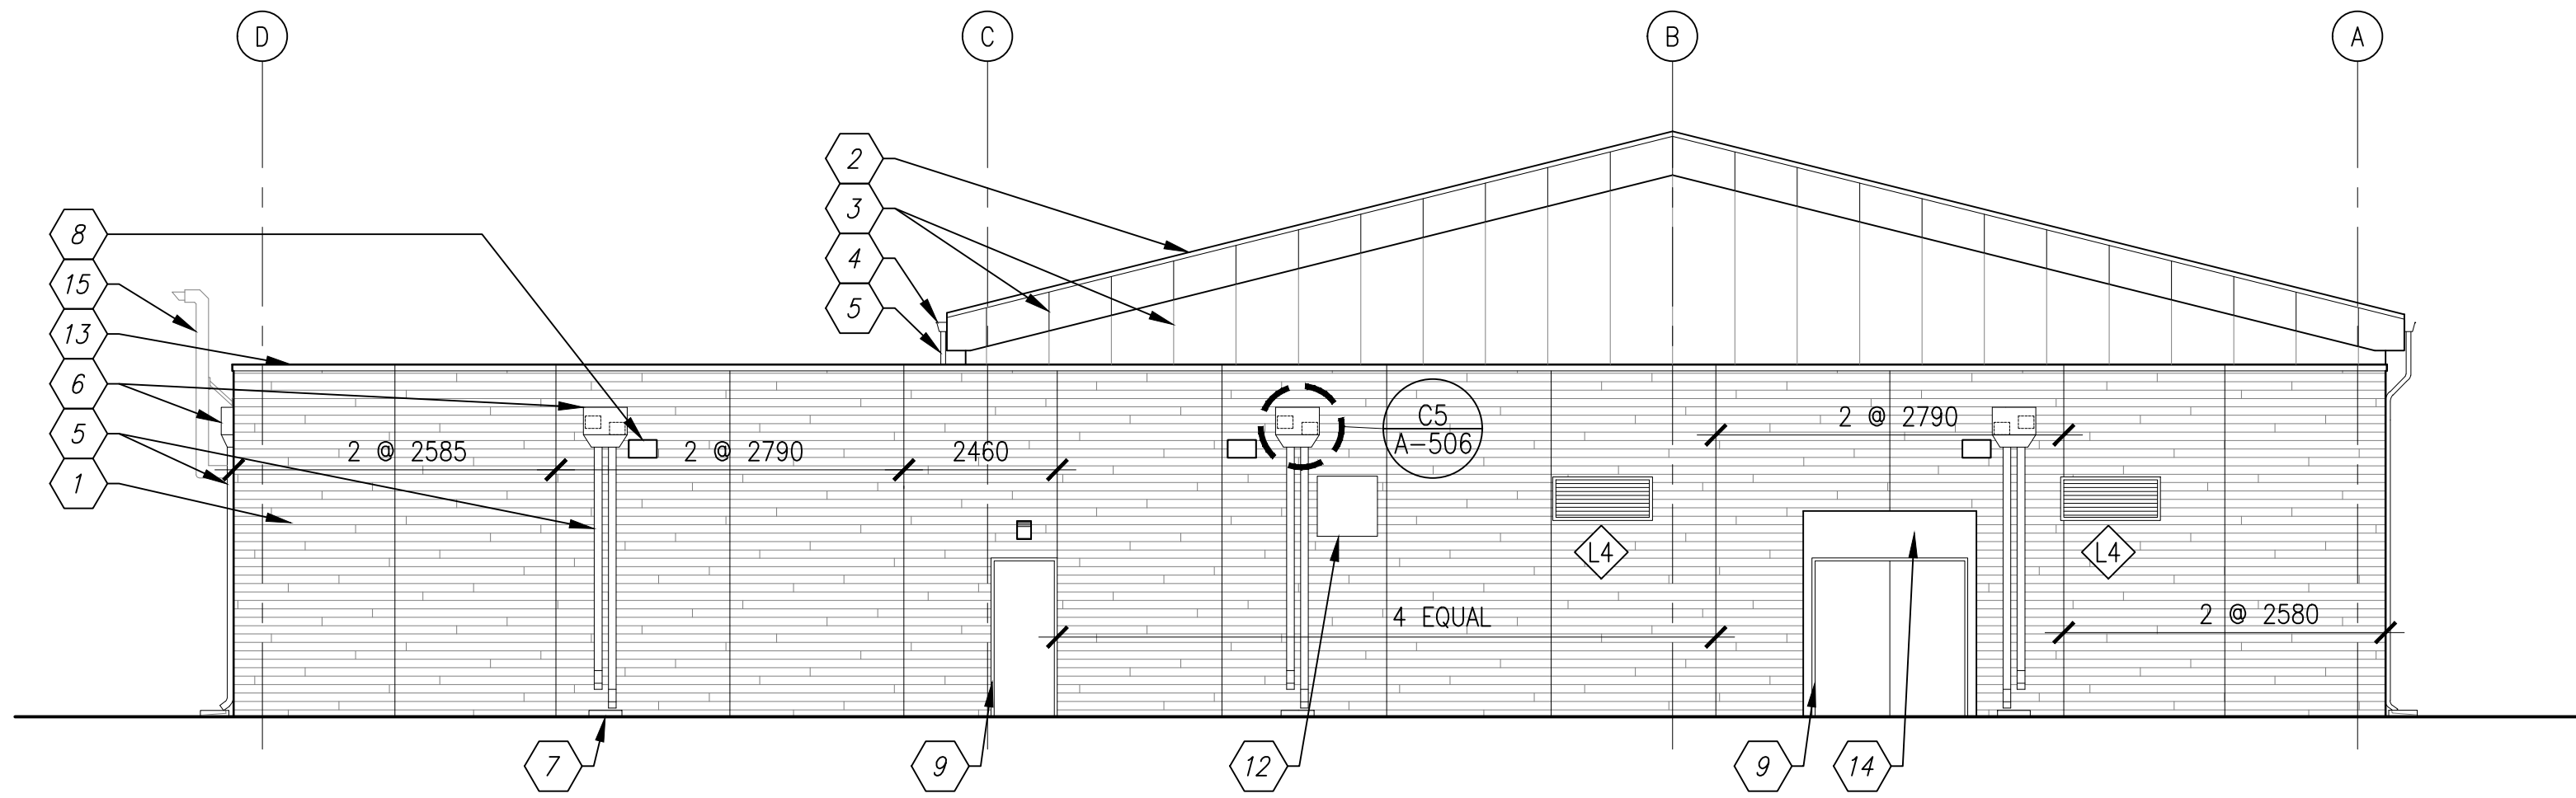

GENERAL SHEET NOTES

- A. REFER TO SHEET A-001 FOR ARCHITECTURAL LEGEND AND ABBREVIATIONS.
- B. REFER TO SHEET A-201 FOR KEYNOTES THIS SHEET.
- C. REFER TO SHEET A-606 FOR WINDOW AND LOUVER SCHEDULE
- D. PROVIDE FIRE RETARDANT TREATED WOOD BLOCKING FOR MOUNTING OF GRAB BARS, WALL MOUNTED CABINETS, AV OR IT EQUIPMENT, AND WHERE NECESSARY FOR PROPER ATTACHMENT OF ITEMS. SECURELY ATTACH BLOCKING TO METAL STUD FLANGES. COORDINATE EXACT LOCATION AND QUANTITY OF BLOCKING WITH EQUIPMENT REQUIRING REINFORCEMENT.
- E. PROVIDE PLYWOOD BACKBOARDS WHERE REQUIRED FOR COMMUNICATIONS EQUIPMENT. ALL EXPOSED EDGES OF BACKBOARD SHALL BE PAINTED ON FIVE SIDES WITH A FIRE RETARDANT PAINT. SEE ELECTRICAL/TELECOM DRAWINGS FOR ADDITIONAL INFORMATION
- F. FINISH FLOOR ELEVATION IS 0.00mm UNLESS OTHERWISE NOTED.
- G. COORDINATE ALL OPENINGS THROUGH INSULATED STRUCTURAL PRECAST SANDWICH PANELS PRIOR TO MANUFACTURING.



APPROVED	A/E INFO
FOR COMMANDER NAVFAC	
ACTIVITY	
SATISFACTORY TO	DATE 01/15/2026
DES PAK	DRW PAK
PM/DM	MJD/ATP
BRANCH MANAGER	KMC
DES PROD DIR	WBF
FIRE PROTECTION ENGINEER	DSN

DEPARTMENT OF THE NAVY
NAVAL FACILITIES ENGINEERING SYSTEMS COMMAND
NAVAL FACILITIES ENGINEERING SYSTEMS COMMAND - ATLANTIC
PLANNING, DESIGN AND CONSTRUCTION
VARIOUS LOCATIONS
VARIOUS LOCATIONS
JOINT MARITIME FACILITY
ELEVATIONS


GRAPHIC SCALE




SCALE:	AS NOTED
APPROVED NO.:	1838720
CONSTR. CONTR. NO.	
NAVFAC DRAWING NO.	14157124
SHEET	62 OF 170
A-205	

FILE NAME: Y:\OCONUS\MultipleSites\2026_1783264-P1360_JAMF\B_Design\DWG\Sheet\08_ARCH\PT1360_1783264_2026.dwg LAYOUT NAME: A-206 ELEVATIONS PLOTTED: Monday, April 20, 2026 - 1:28pm USER: paulakeller1

B1 SOUTH ELEVATION
SCALE: 1:100

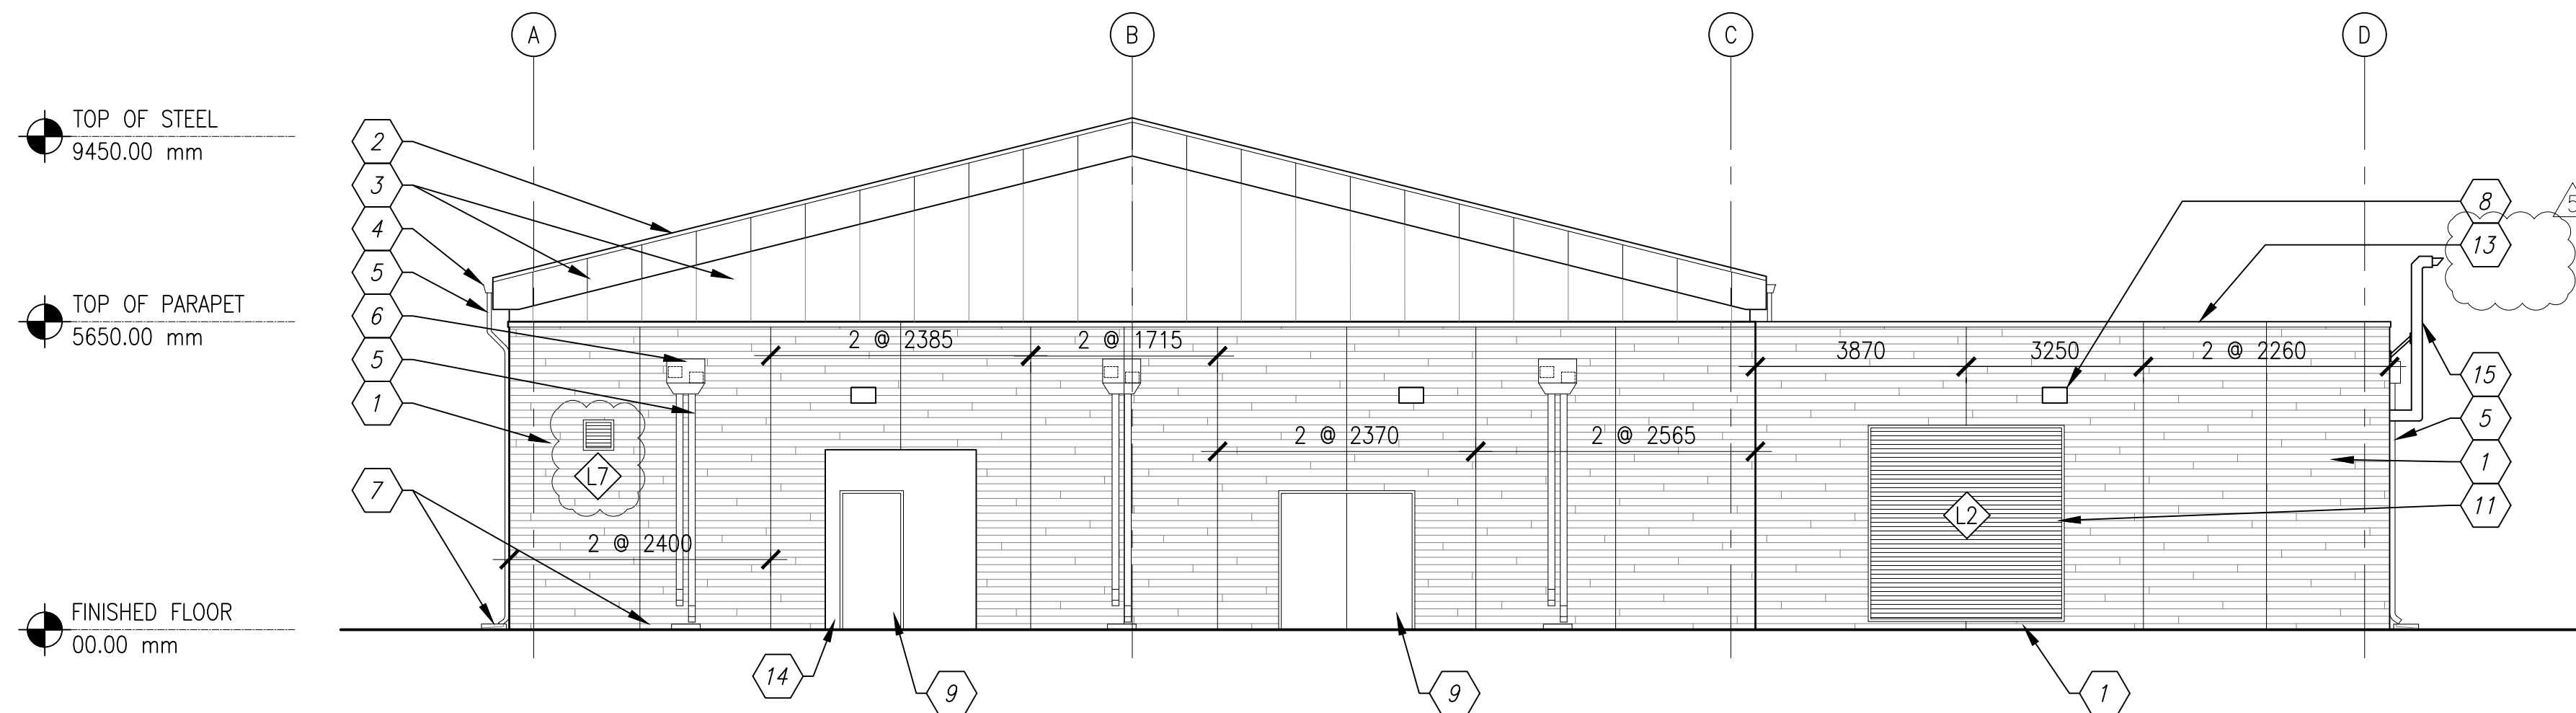


A1 EAST ELEVATION
SCALE: 1:100

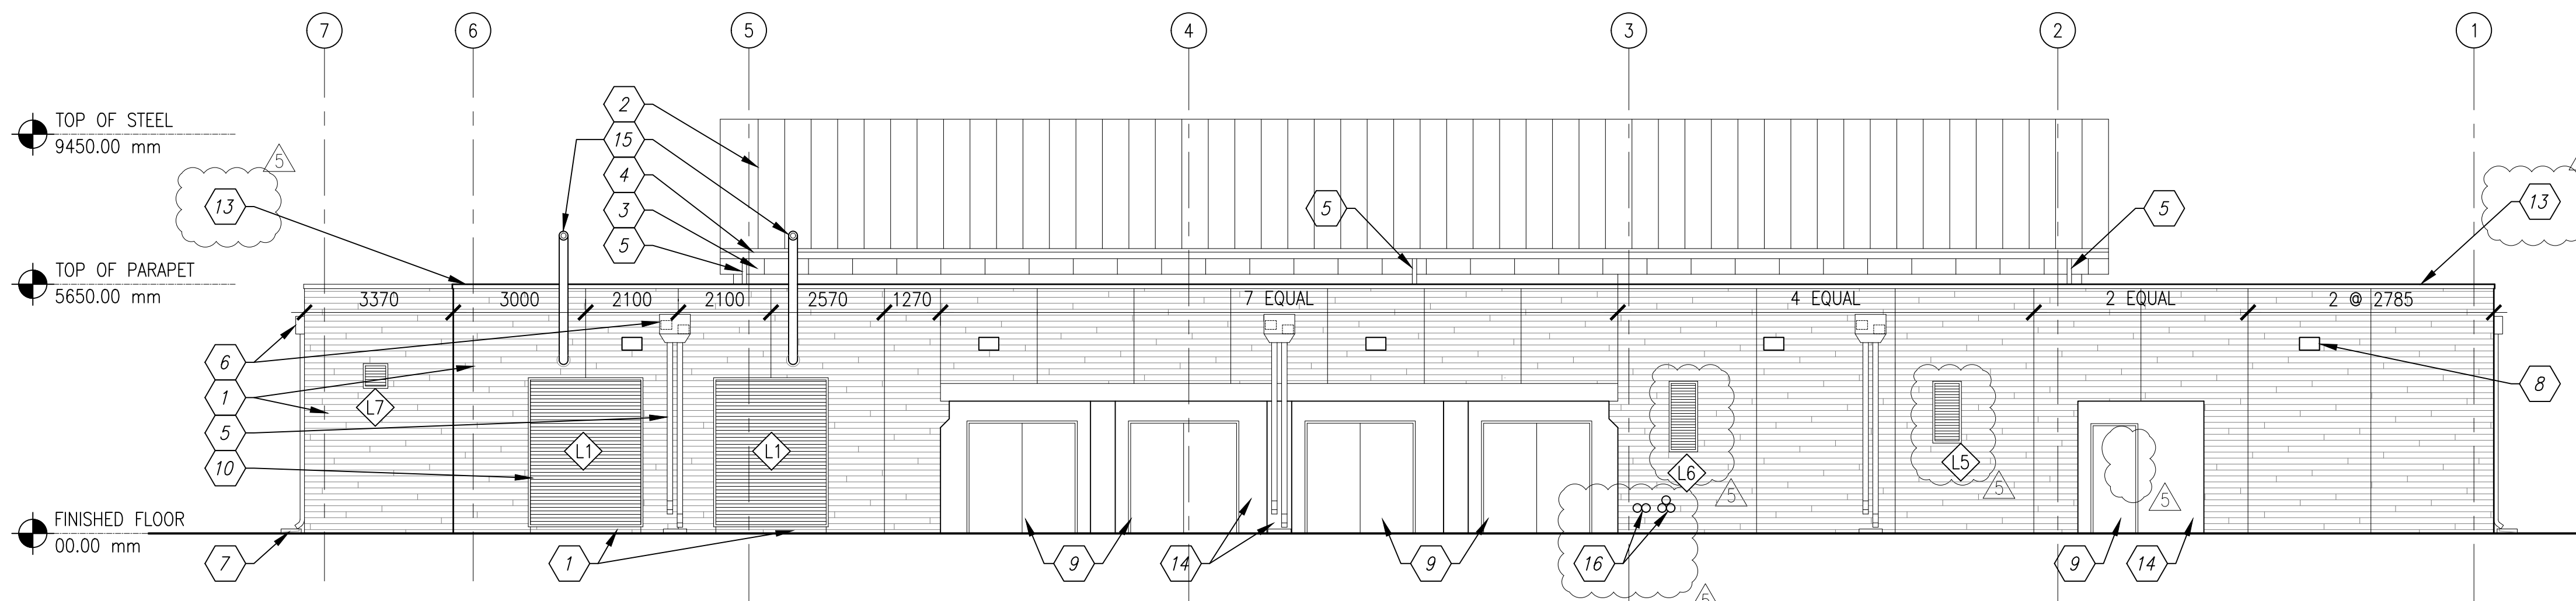

GENERAL SHEET NOTES

- REFER TO SHEET A-001 FOR ARCHITECTURAL LEGEND AND ABBREVIATIONS.
- REFER TO SHEET A-201 FOR KEYNOTES THIS SHEET.
- REFER TO SHEET A-606 FOR WINDOW AND LOUVER SCHEDULE
- PROVIDE FIRE RETARDANT TREATED WOOD BLOCKING FOR MOUNTING OF GRAB BARS, WALL MOUNTED CABINETS, AV OR IT EQUIPMENT, AND WHERE NECESSARY FOR PROPER ATTACHMENT OF ITEMS. SECURELY ATTACH BLOCKING TO METAL STUD FLANGES. COORDINATE EXACT LOCATION AND QUANTITY OF BLOCKING WITH EQUIPMENT REQUIRING REINFORCEMENT.
- PROVIDE PLYWOOD BACKBOARDS WHERE REQUIRED FOR COMMUNICATIONS EQUIPMENT. ALL EXPOSED EDGES OF BACKBOARD SHALL BE PAINTED ON FIVE SIDES WITH A FIRE RETARDANT PAINT. SEE ELECTRICAL/TELECOM DRAWINGS FOR ADDITIONAL INFORMATION
- FINISH FLOOR ELEVATION IS 0.00mm UNLESS OTHERWISE NOTED.
- COORDINATE ALL OPENINGS THROUGH INSULATED STRUCTURAL PRECAST SANDWICH PANELS PRIOR TO MANUFACTURING.

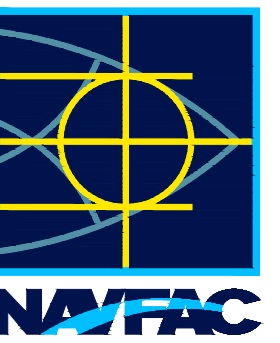

APPROVED
FOR COMMANDER NAVFAC
ACTIVITY
D. EVANS VIA EMAIL
SATISFACTORY TO DATE 01/15/2026
DES PAK DRW PAK CHK JHR
PM/DM MJD/ATP
BRANCH MANAGER KMC
DES PROD DIR WBF
FIRE PROTECTION ENGINEER DSN


DEPARTMENT OF THE NAVY
NAVAL FACILITIES ENGINEERING SYSTEMS COMMAND
NAVAL FACILITIES ENGINEERING SYSTEMS COMMAND - ATLANTIC
PLANNING, DESIGN AND CONSTRUCTION
VARIOUS LOCATIONS
VARIOUS LOCATIONS
JOINT MARITIME FACILITY
ELEVATIONS

SCALE: AS NOTED
APPROVED NO.: 1838720
CONSTR. CONTR. NO.
NAVFAC DRAWING NO.: 14157125
SHEET 63 OF 170
A-206


NAVFAC METRIC DRAWING REVISION: 01 OCTOBER 2018

FILE NAME: Y:\OCONUS\MultipleSites\2026_1783264_P1360_IAMF\B_Design\DWGS\Sheet\08_ARCH\PT1360_1783264_4606.dwg LAYOUT NAME: A-606 DOOR AND WINDOW SCHEDULES AND TYPES PLOTTED: Monday, April 20, 2026 - 1:30pm USER: paulakelert

DOOR SCHEDULE																	
DOOR							FRAME						FIRE RATING (MIN.)	HARDWARE		NOTES	MARK
MARK	SIZE			MATL	DOOR TYPE	GLZ	MATL	FRAME TYPE	GLZ	DETAILS				SET NO	KEYSIDE RM NO		
	W	HT	THK							HEAD	JAMB	THRESHOLD					
100A	965	2150	45	HM	D1	--	ALUM	F1	--	D1/A-607	A1/A-607	C1/A-607	--	1.0	--	2, 3, 6	100A
100B	965	2150	45	HM	D1	--	HM	F1	--	A3/A-607	A3/A-607		120	6.0	100		100B
100C	965	2150	45	HM	D1	--	HM	F1	--	A4/A-607	A4/A-607		120	8.0	100	1, 3	100C
102	965	2150	45	HM	D1	--	HM	F1	--	D1/A-607	A1/A-607	C1/A-607	--	1.1	--	6	102
103	965	2150	45	HM	D1	--	HM	F1	--	A3/A-607	A3/A-607		--	4.0	--	4	103
104	965	2150	45	HM	D1	--	HM	F1	--	A3/A-607	A3/A-607		--	4.0	--	4	104
105	965	2150	45	HM	D1	--	HM	F1	--	A3/A-607	A3/A-607		--	5.0	--	4	105
106	915	2150	45	HM	D1	--	HM	F1	--	A3/A-607	A3/A-607		S	3.0	--	4	106
107	965	2150	45	HM	D1	--	HM	F1	--	A3/A-607	A3/A-607		S	4.1	--	5	107
108	965	2150	45	HM	D1	--	HM	F1	--	A3/A-607	A3/A-607		S	4.1	--	5	108
109A	2400	2450	45	HM	D2	--	HM	F2	--	D2/A-607	A2/A-607	C1/A-607	--	2.1	109	1, 2, 3, 6	109A
109B	915	2150	45	HM	D1	--	HM	F1	--	A3/A-607	A3/A-607		S	6.1	101		109B
109C	2400	2450	45	HM	D2	--	HM	F2	--	D4/A-607	D4/A-607	B4/A-607	60	7.0	--	3	109C
110	915	2450	45	HM	D1	--	HM	F1	--	A3/A-607	A3/A-607		60	3.4	--		110
111A	965	2150	45	HM	D1	--	HM	F1	--	D3/A-607	D3/A-607		60	8.3	111	1, 3	111A
111B	965	2150	45	HM	D1	--	HM	F1	--	D1/A-607	A1/A-607	C1/A-607	--	1.0	--	2, 3, 6	111B
111C	965	2150	45	HM	D1	--	HM	F1	--	D3/A-607	D3/A-607		120	3.6	--		111C
112A	2400	2450	45	HM	D2	--	HM	F2	--	D2/A-607	A2/A-607	C1/A-607	--	2.0	112	2, 3, 6	112A
112B	1200	2150	45	HM	D1	--	HM	F1	--	A3/A-607	A3/A-607		S	3.5	--		112B
113A	2400	2450	45	HM	D2	--	HM	F2	--	D2/A-607	A2/A-607	C1/A-607	120	2.0	113	2, 3, 6	113A
113B	965	2150	45	HM	D1	--	HM	F1	--	A4/A-607	A4/A-607		60	3.1	111		113B
114A	2400	2450	45	HM	D2	--	HM	F2	--	D2/A-607	A2/A-607	C1/A-607	180	2.0	114	2, 3, 6	114A
114B	2400	2450	45	HM	D2	--	HM	F2	--	D2/A-607	A2/A-607	C1/A-607	180	2.0	114	2, 3, 6	114B
115A	915	2150	45	HM	D1	--	HM	F1	--	B5/A-607	B5/A-607		180	3.1	115		115A
115B	1200	2150	45	HM	D1	--	HM	F1	--	A5/A-607	A5/A-607		120	3.3	111	1	115B
116A	1200	2150	45	HM	D1	--	HM	F1	--	D3/A-607	D3/A-607	B3/A-607	60	8.1	101	1, 3	116A
116B	965	2150	45	HM	D1	--	HM	F1	--	D3/A-607	D3/A-607	B3/A-607	60	8.2	--	1, 3	116B
117	1200	2450	45	HM	D1	--	HM	F1	--	A3/A-607	A3/A-607		60	3.2	117		117
118A	1200	2450	45	HM	D1	--	HM	F1	--	A3/A-607	A3/A-607		60	3.2	118		118A
118B	2400	2450	45	HM	D2	--	HM	F1	--	D2/A-607	A2/A-607	C1/A-607	--	2.0	118	2, 3, 6	118B
119	1200	2450	45	HM	D1	--	HM	F1	--	A3/A-607	A3/A-607		60	3.2	119		119

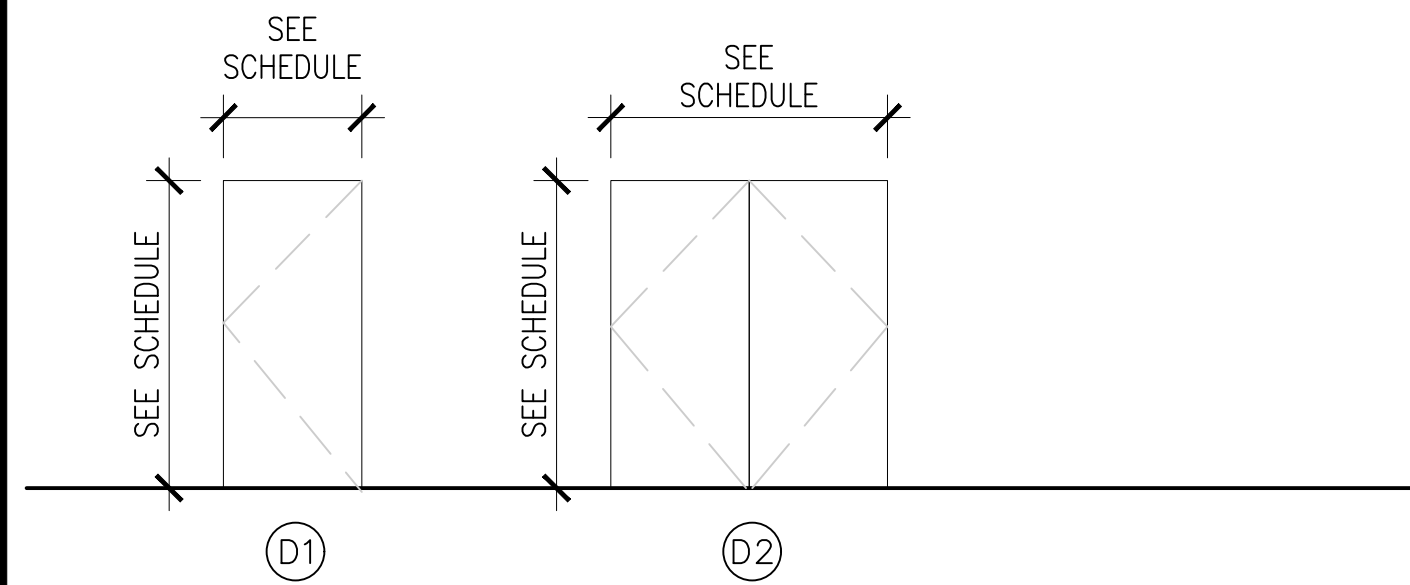


B1 DOOR TYPES
SCALE: 1:50
A-606

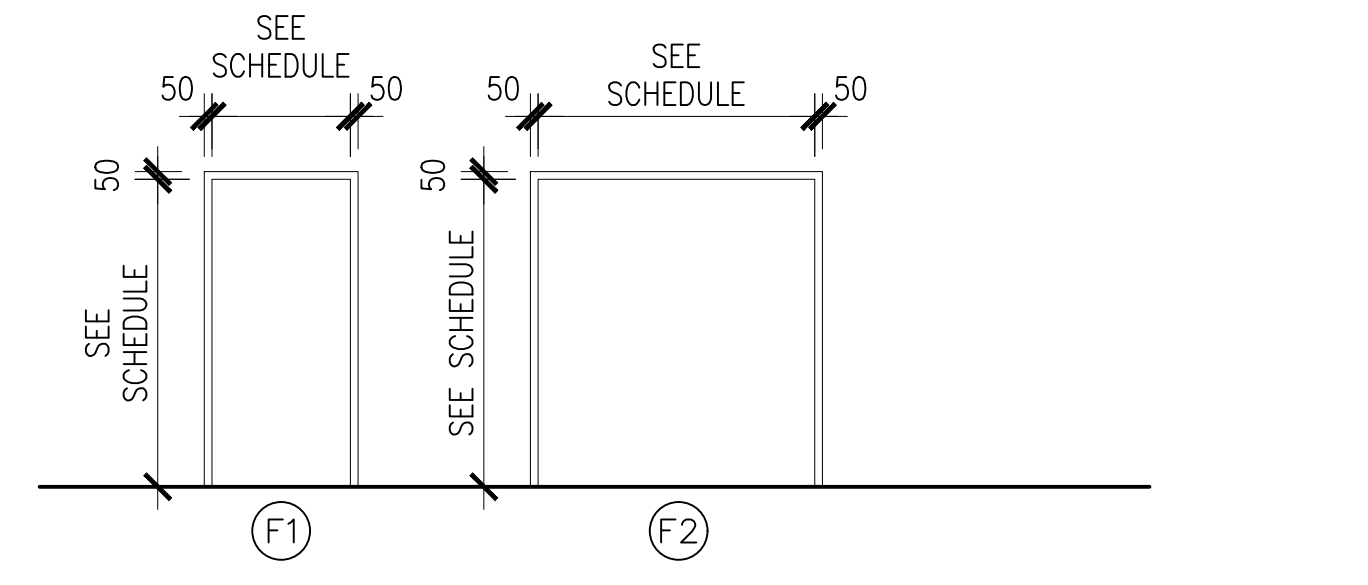

B2 DOOR TYPES
SCALE: 1:50
A-606

LOUVER SCHEDULE		
MARK ON DWGS	DESCRIPTION	BOTTOM OF LOUVER ROUGH OPENING
L-1	HORIZONTAL BLADES	300 MM AFF
L-2	HORIZONTAL BLADES	300 MM AFF
L-3	HORIZONTAL BLADES	3060 MM AFF
L-4	HORIZONTAL BLADES	3200 MM AFF
L-5	HORIZONTAL BLADES	2180 MM AFF
L-6	HORIZONTAL BLADES	2380 MM AFF
L-6	HORIZONTAL BLADES	3340 MM AFF

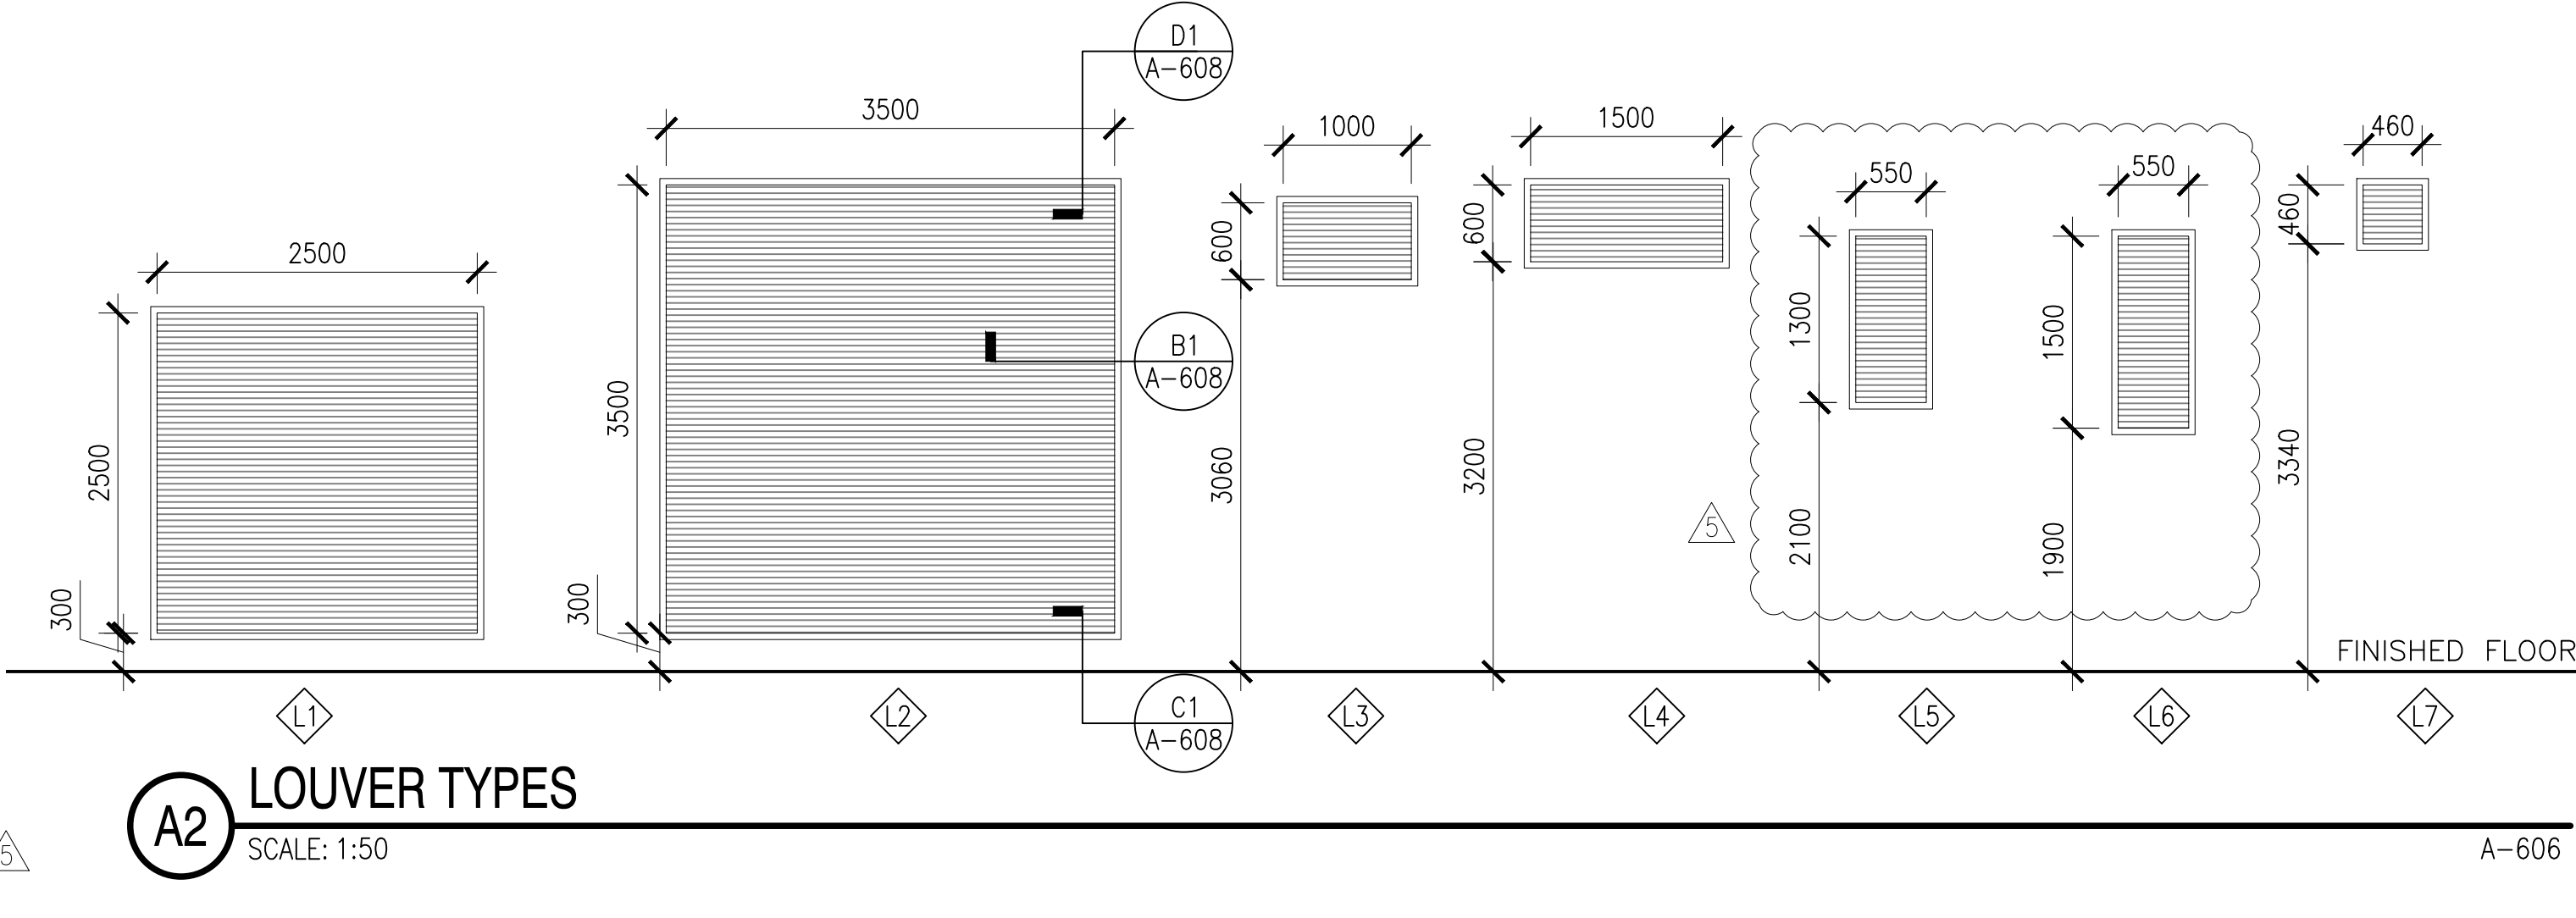

A2 LOUVER TYPES
SCALE: 1:50
A-606

GENERAL DOOR NOTES	
1	PROVIDE INSULATION WITHIN EXTERIOR DOOR ASSEMBLIES.
2	REFER TO FINISH SCHEDULE FOR DOOR AND FRAME FINISHES.
3	REFER TO UFGS 08 71 00 DOOR HARDWARE FOR DOOR HARDWARE SET SCHEDULE.
4	PROVIDE DOOR HARDWARE TO MEET REQUIRED DOOR RATING
5	STC 45 DOOR/FRAME ASSEMBLIES IN STUD WALLS REQUIRE STRUCTURAL STEEL REINFORCEMENT HIDDEN ENTIRELY WITHIN WALL. REFER TO DOOR DETAILS AND STRUCTURAL DRAWINGS.
DOOR SCHEDULE NOTES	
1	PROVIDE STC 45 ACOUSTICAL DOOR ASSEMBLY – REFER TO 08 34 73 SOUND CONTROL DOOR ASSEMBLIES FOR ADDITIONAL INFORMATION.
2	DOOR FRAME DEPTH: MIN 200MM
3	PREP DOOR AND DOOR FRAME FOR ACCESS CONTROL SYSTEM – SEE ELECTRONIC SECURITY SYSTEM DRAWINGS.
4	REFER TO INTERIOR DRAWINGS FOR FLOOR TRANSITION DETAIL AT SILL
5	PROVIDE STC 35 ACOUSTICAL DOOR ASSEMBLY – REFER TO 08 34 73 SOUND CONTROL DOOR ASSEMBLIES FOR ADDITIONAL INFORMATION.
6	PROVIDE HURRICANE-RESISTANT DOOR ASSEMBLY.
SCHEDULE ABBREVIATIONS	
HM	HOLLOW METAL (PRIMED)
STL	STEEL
WD	WOOD

APPR

DATE

04/21/26

03/27/26

REMOVED GLAZING SCHEDULE, UPDATED L5/L6 LOWERS

DOOR 110 FIRE RATING UPDATE

SYN

DESCRIPTION

SEAL

A/E INFO

APPROVED

FOR COMMANDER NAVFAC

ACTIVITY

D. EVANS VIA EMAIL

SATISFACTORY TO DATE 01/15/2026

DES PAK DRW PAK LCHK JHR

PM/DM MJD/ATP

BRANCH MANAGER KMC

DES PROD DIR WBF

FIRE PROTECTION ENGINEER DSN

DEPARTMENT OF THE NAVY

NAVAL FACILITIES ENGINEERING SYSTEMS COMMAND

NAVAL FACILITIES ENGINEERING SYSTEMS COMMAND - ATLANTIC

PLANNING, DESIGN AND CONSTRUCTION

VARIOUS LOCATIONS

VARIOUS LOCATIONS

JOINT MARITIME FACILITY

DOOR AND WINDOW SCHEDULES AND TYPES

SCALE: AS NOTED

APPROVED NO. 1838720

CONSTR. CONTR. NO.

NAVFAC DRAWING NO. 14157145

SHEET 83 OF 170

A-606

NAVFAC METRIC DRAWFORM REVISION: 01 OCTOBER 2018

FILE NAME: C:\Users\elizabeth.clemens\AppData\Local\Temp\AcPublish_26468\PT130_1753264_IN601.dwg LAYOUT NAME: IN601 INTERIOR FINISH LEGEND AND SCHEDULE PLOTTED: Monday, April 20, 2026 - 11:00am USER: elizabeth.clemens

D


C

B


A

FINISH LEGEND					
CODE	MATERIAL	BASIS OF DESIGN PRODUCT	COLOR	SIZE	NOTES
FLOORS					
ESD1	ESD FLOOR TILE	FORBO COLOREX EC	EC 250201 EVEREST	24" x 24"	INSTALL WITH RAF1
PT1	PORCELAIN TILE	CROSSVILLE COLOR BLOX 2.0	CBX03 SLINKY	12" x 24"	
PT4	PORCELAIN TILE (MOSAIC)	CROSSVILLE COLOR BLOX 2.0	CBX03 SLINKY	3" x 3"	
RAF1	RAISED ACCESS FLOOR SYSTEM	TATE 2"D BOLTED STRINGER UNDERSTRUCTURE, CONCORE 3000 FLOOR PANELS	---	24" x 24"	2'-0" FINISHED FLOOR HEIGHT, INSTALL WITH ESD1
SC1	SEALED CONCRETE	ASHFORD FORMULA	CLEAR	--	
SC2	SEALED CONCRETE, ANTISTATIC	ELECTRASEAL ANTI STATIC CONCRETE SEALER	CLEAR	--	
WALL BASE					
PTB1	PORCELAIN TILE BASE	CROSSVILLE COLOR BLOX 2.0	CBX03 SLINKY	12" x 6" HIGH	COVE BASE
RB1	RUBBER BASE	ROPPE	123 CHARCOAL	6" HIGH	STANDARD TOE BASE
WALLS					
PT2	PORCELAIN TILE (FIELD WALL TILE)	CROSSVILLE COLOR BLOX 2.0	CBX03 SLINKY	12" x 24"	INSTALL ALUMINUM FINISH EDGE AT ALL INTERIOR AND EXTERIOR CORNERS
PT3	PORCELAIN TILE (ACCENT WALL TILE)	CROSSVILLE COLOR BLOX 2.0	CBX31 COTTON SHEETS	6" x 6"	INSTALL ALUMINUM FINISH EDGE AT ALL INTERIOR AND EXTERIOR CORNERS
PNT1	WALL PAINT	SHERWIN WILLIAMS	SW7063 NEBULOUS WHITE	---	
SS1	SOLID SURFACE SHOWER WALL PANELS	SWANSTONE	WHITE	FULL HEIGHT	INSTALL PER MANUFACTURER'S INSTRUCTIONS
CEILINGS					
ACT1	ACOUSTIC CEILING TILE	ARMSTRONG, CALLA HIGH NRC, TEGULAR	WHITE	24" x 24"	INSTALL WITH ACG1
ACT2	CLEAN-ROOM ACOUSTIC CEILING TILE	ARMSTRONG, CALLA FOR DYNAMAX, SQUARE LAY-IN	WHITE	24" x 24'	INSTALL WITH ACG2
ACT3	PERFORATED AIR DEVICE TILE	PRICE, PERFORATED AIR DEVICE MODEL 10	WHITE	24" x 24"	INSTALL AS REQUIRED, SEE MECHANICAL DRAWINGS FOR LOCATIONS
ACG1	ACOUSTIC CEILING GRID	ARMSTRONG, TEGULAR 15/16" GRID	WHITE	15/16"	INCLUDE SEISMIC SUPPORTS
ACG2	STRUCTURAL CEILING GRID	ARMSTRONG DYNAMAX	WHITE	24"x24"x2"	INCLUDE SEISMIC SUPPORTS
PNT2	DRYWALL CEILING PAINT	SHERWIN WILLIAMS	SW7007 CEILING BRIGHT WHITE	--	
PNT3	DRY-FALL PAINT	SHERWIN WILLIAMS	SW7007 CEILING BRIGHT WHITE	--	
MISCELLANEOUS					
CG1	CORNER GUARD	CS GROUP, CO-8	TYPE 304 STAINLESS STEEL #4 FINISH	3-1/2" LEGS	INSTALL ON ALL OUTSIDE CORNERS, BOTTOM OF CORNER GUARD TO ALIGN WITH TOP OF WALL BASE, FULL HEIGHT OF WALL
GRT1	GROUT	MAPEI	112 MEDIUM GREY	3/16" JOINT	INSTALL WITH PT1, PT2, PT3, AND PTB1
LKR1	PHENOLIC LOCKERS	BRADLEY CORP. PHENOLIC LOCKER	SLATE GREY D91		FULL HEIGHT
PLAM1	PLASTIC-LAMINATE CASEWORK	WILSONART	7919K-78 AMBER CHERRY		
PNT4	DOOR & TRIM PAINT	SHERWIN WILLIAMS	SW7067 CITYSCAPE		
SS2	SOLID SURFACE COUNTERTOPS	CORIAN	MATTERHORN		
SS3	SOLID SURFACE SHOWER PAN	SWANSTONE	WHITE		
SG1	SIGNAGE	2/90 SIGN SYSTEMS, SLIDE MODULAR	211 ASH/233 PEARL GREY		INCLUDE SATIN NATURAL ALUMINUM TRIM


FINISH SCHEDULE										
MARK	NAME	FLOOR		BASE		WALL		CEILING		NOTES
		FINISH	COLOR	FINISH	COLOR	FINISH	COLOR	FINISH	COLOR	
100	SECURE VESTIBULE	SC	2	RB	1	PNT	1	ACG/ACT	1/1	--
101	OPEN OFFICE	SC	2	RB	1	PNT	1	ACG/ACT	1/1	--
102	UNSECURE CORRIDOR	SC	1	RB	1	PNT	1	ACG/ACT	1/1	--
103	SHOWER	PT	4	PTB	1	PT	2/3	GWB/PNT	2	1
104	TOILET	PT	1	PTB	1	PT	2/3	GWB/PNT	2	--
105	BREAK	PT	1	PTB	1	PNT	1	ACG/ACT	1/1	--
106	JANITOR	SC	1	RB	1	PNT	1	GWB/PNT	2	--
107	BUNK	SC	1	RB	1	PNT	1	ACG/ACT	1/1	--
108	BUNK	SC	1	RB	1	PNT	1	ACG/ACT	1/1	--
109	STAGING AREA	SC	2	RB	1	PNT	1	EXP/PNT	3	--
110	COMMERCIAL TELECOM	SC	2	RB	1	PNT	1	EXP/PNT	3	--
111	CORRIDOR	SC	2	RB	1	PNT	1	ACG/ACT	1/1	--
112	MECHANICAL	SC	1	RB	1	PNT	1	EXP/PNT	3	--
113	FIRE PUMP	SC	1	RB	1	PNT	1	EXP/PNT	3	--
114	GENERATOR FUEL ROOM	SC	1	RB	1	EXP	--	EXP/PNT	3	--
115	GENERATOR ROOM	SC	1	RB	1	PNT	1	EXP/PNT	3	--
116	OPS EQUIPMENT	SC/RAF/ESD	1/1/1	RB	1	PNT	1	GWB/PNT/ACG/ACT/ACT	-/2/2/2/3	--
117	UPS A	SC	2	RB	1	PNT	1	EXP/PNT	3	--
118	ELECTRICAL	SC	2	RB	1	PNT	1	EXP/PNT	3	--
119	UPS B	SC	2	RB	1	PNT	1	EXP/PNT	3	--

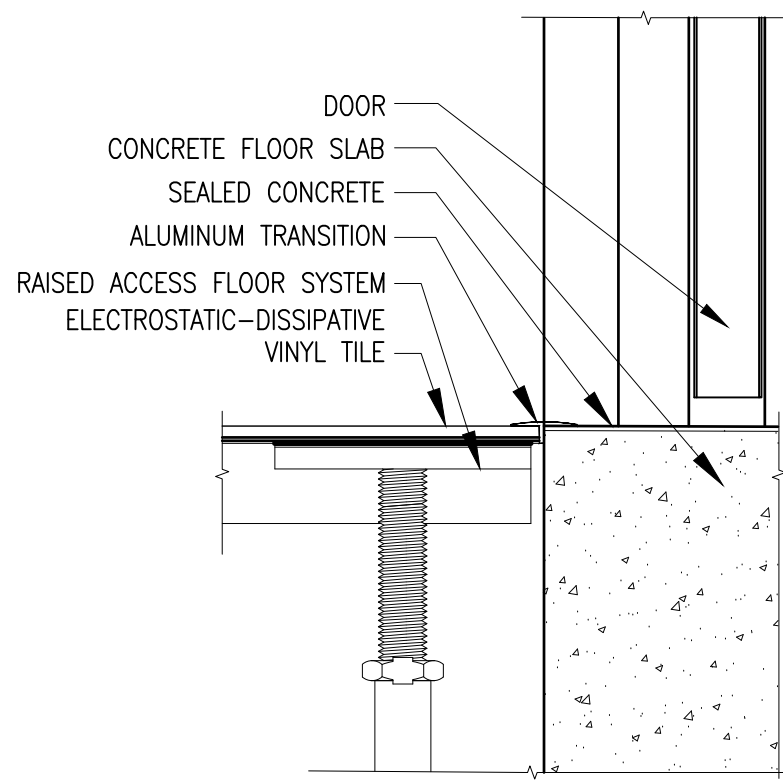

D4 RAF TRANSITION
SCALE: 1:5 IN601

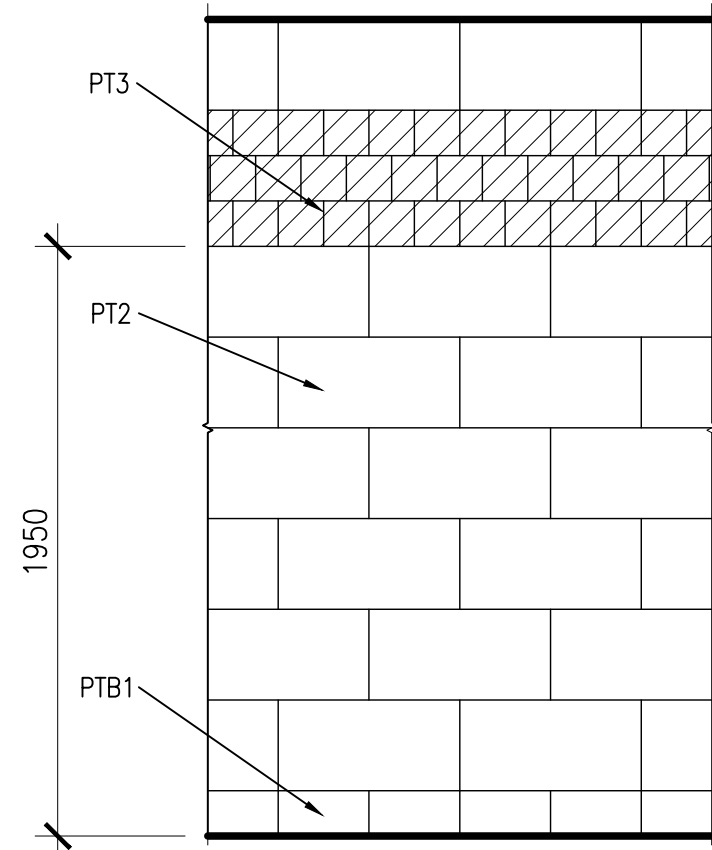

C4 ACCENT WALL TILE ELEVATION
SCALE: 1:25 IN601

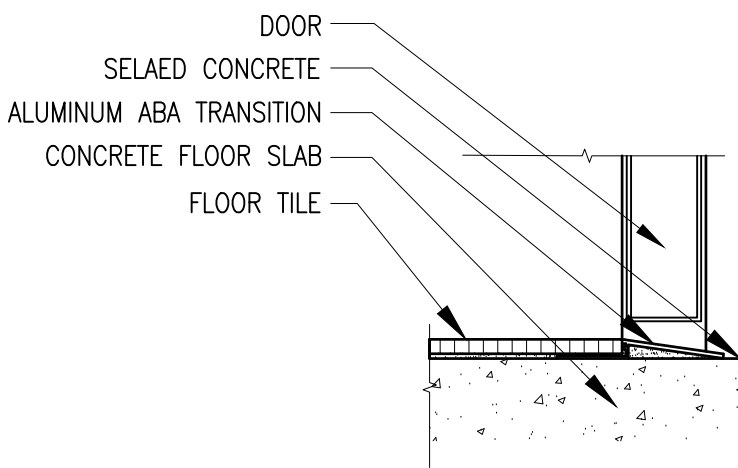

B4 PT TO SC TRANSITION
SCALE: 1:5 IN601

GENERAL SHEET NOTES

- THE USE OF MANUFACTURER'S NAMES AND PRODUCT NUMBERS IS NOT INTENDED TO BE PROPRIETARY. OTHER MANUFACTURER'S PRODUCTS WILL BE CONSIDERED, PROVIDED THEY CLOSELY APPROXIMATE COLOR, FINISH, TEXTURE, PATTERN AND QUALITY.
- CONTRACTOR MUST CHECK AND COORDINATE LEAD TIMES AND REQUIREMENTS FOR ALL FINISHES ON FINISH LEGEND PRIOR TO ORDERING.
- PROVIDE STAINLESS STEEL METAL TRANSITION STRIPS BETWEEN DISSIMILAR FLOOR FINISHES. TRANSITION STRIPS TO BE CENTERED UNDER DOORS AS APPLICABLE.
- PROVIDE ALUMINUM FINISH EDGE AT ALL INSIDE AND OUTSIDE CORNERS AT WALL TILE.
- PROVIDE STAINLESS STEEL CORNER GUARDS AT ALL OUTSIDE CORNERS. MOUNT BOTTOM OF CORNER GUARD AT TOP OF WALL BASE.
- ALIGN ALL FLOOR AND WALL TILE GROUT JOINTS TO THE GREATEST EXTENT POSSIBLE.
- PROVIDE PAINT FINISHES AS FOLLOWS: FLAT FINISH ON CEILINGS, EGGSHELL FINISH ON WALLS, AND SEMI-GLOSS FINISH ON DOORS AND DOOR TRIM.
- REFER TO A-106 FOR CEILING HEIGHTS.
- ALL EXPOSED SURFACES MUST BE PAINTED, INCLUDING, BUT NOT LIMITED TO, STRUCTURAL STEEL, COLUMNS, TRUSSES, JOINTS, GRTS, AND METAL DECK.
- EXTEND FLOOR FINISH UNDER CASEWORK.
- ALIGN LENGTH OF FLOOR TILE TO RUN PARALLEL WITH LENGTH OF ROOM.



FINISH SCHEDULE NOTES


- SHOWER PAN TO BE SS3 AND SHOWER WALLS TO BE SS1.

GRAPHIC SCALE

1:25 0 500 1500 2500mm

1:5 0 100 300 500mm

APPR	DATE	04/21/26
SYN	DESCRIPTION	AMENDMENT 5
SEAL		
A/E RPTD		
APPROVED		
FOR COMMANDER NAVFAC		
ACTIVITY		
D. EVANS VIA EMAIL		
SATISFACTORY TO DATE 01/15/2026		
DES	ELC	ELC
DRW	ELC	ELC
CHK	ELC	ELC
APP	ELC	ELC
PM/DM	MJD/ATP	
BRANCH MANAGER	KEVIN COYNE, RA	
DES PROD DIR	WBF	
FIRE PROTECTION ENGINEER	DSN	
DEPARTMENT OF THE NAVY	NAVAL FACILITIES ENGINEERING SYSTEMS COMMAND	NAVAL FACILITIES ENGINEERING SYSTEMS COMMAND - ATLANTIC
PLANNING, DESIGN AND CONSTRUCTION	VARIOUS LOCATIONS	VARIOUS LOCATIONS
JOINT MARITIME FACILITY	INTERIOR FINISH LEGEND AND SCHEDULE	
SCALE:	AS NOTED	
APPROVED NO.:	1838720	
CONSTR. CONTR. NO.:		
NAVFAC DRAWING NO.:	14157152	
SHEET	90	OF 170
IN601		

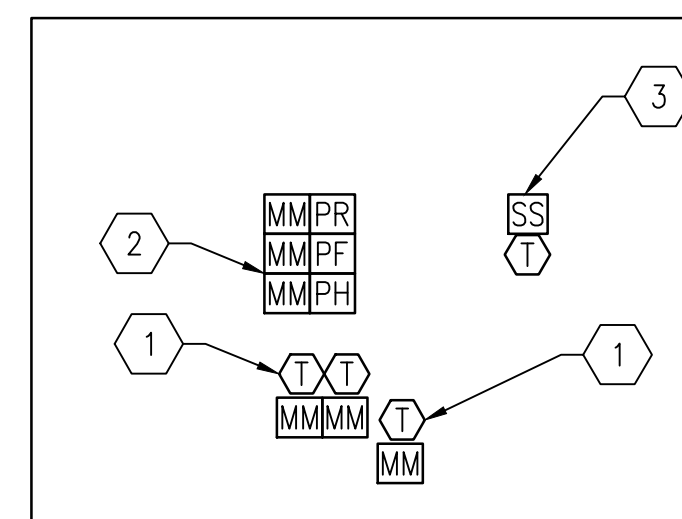


A3 FIRE ALARM PUMP ROOM 113
SCALE: 1:100

GRAPHIC SCALE

- 1:100 0 1000 5000 10000mm

VEAC METRIC DRAWFORM REVISION: 01 OCTOBER 20

FILE NAME: Y:\CONUS\MultipleStations\2026_1783264_P1360_JAMF\B_Design\DWG\Sheet\13_ELEC\1360_1783264_EP102 - AMEND 3.dwg LAYOUT NAME: EP102 - Electrical Power Plan - Mechanical Equipment PLOTTED: Monday, April 20, 2026 - 14:3pm USER: onmpriest

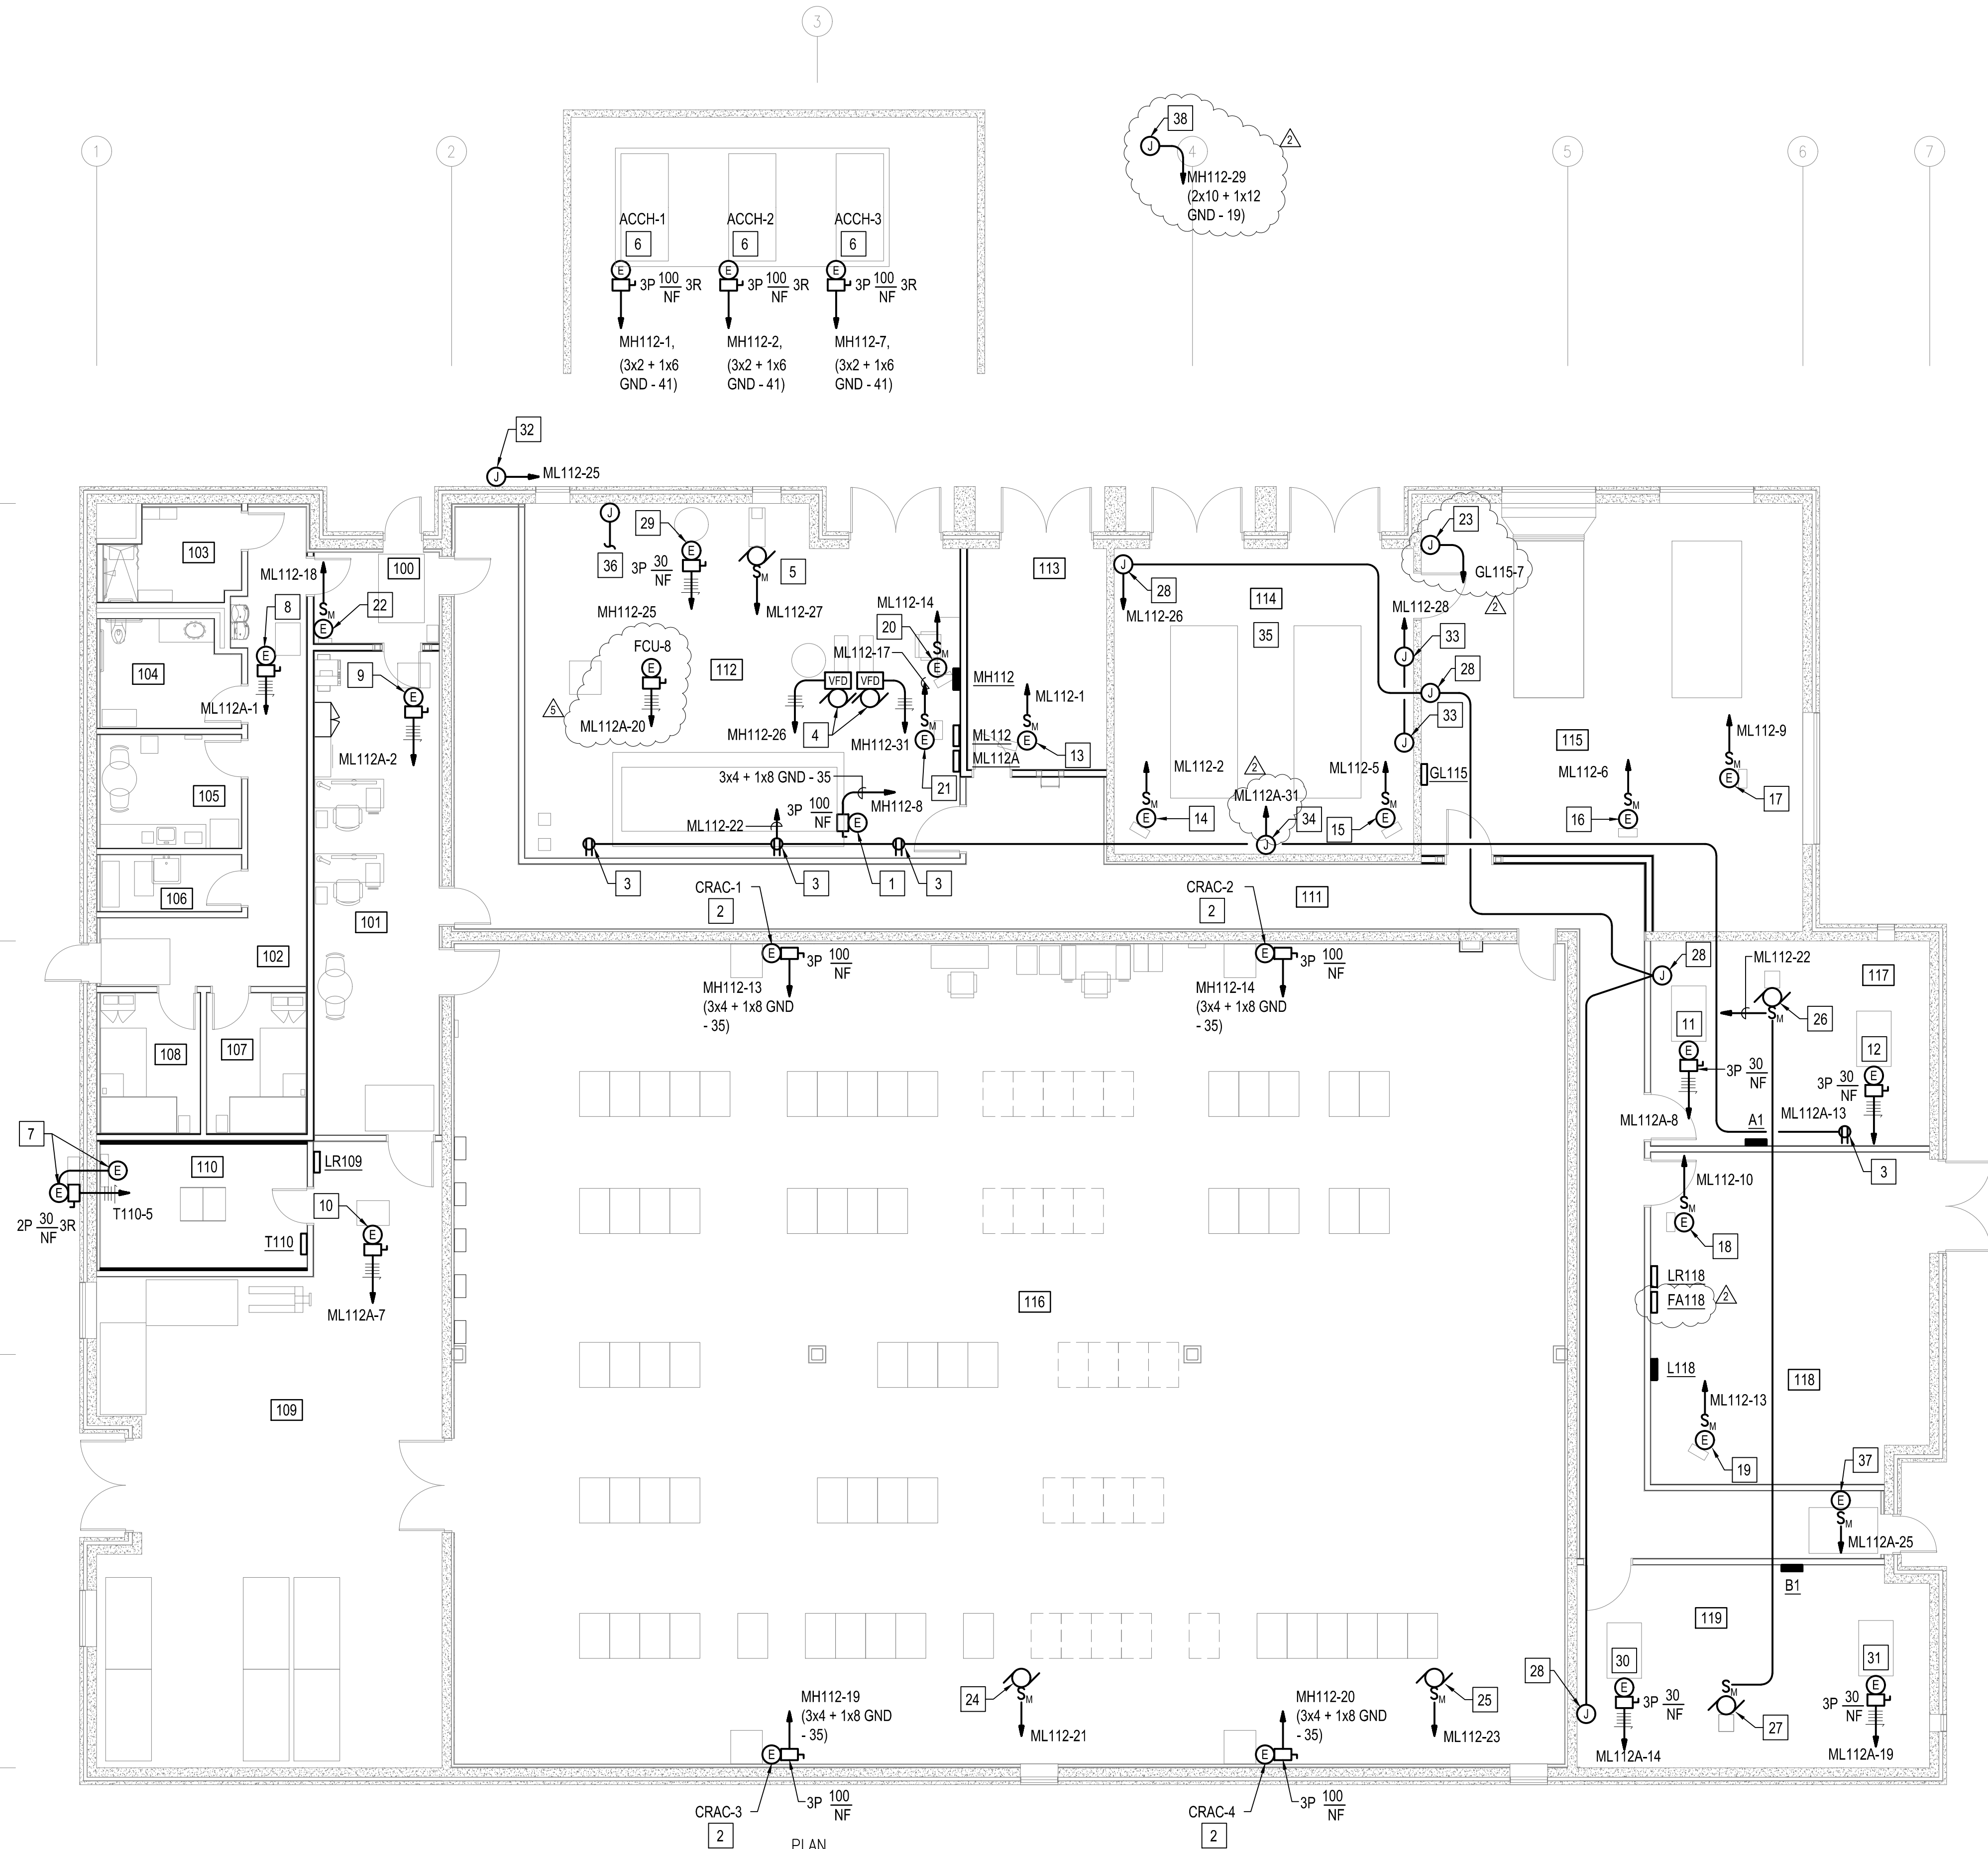



110 DOOR DESIGNATION

162 ROOM DESIGNATION

- 110 DOOR DESIGNATION
- 162 ROOM DESIGNATION

A1 VIDEO SURVEILLANCE SYSTEM RISER DIAGRAM 3

SCALE: NONE

[illegible]