


LARGE BERM DETAIL

NO SCALE

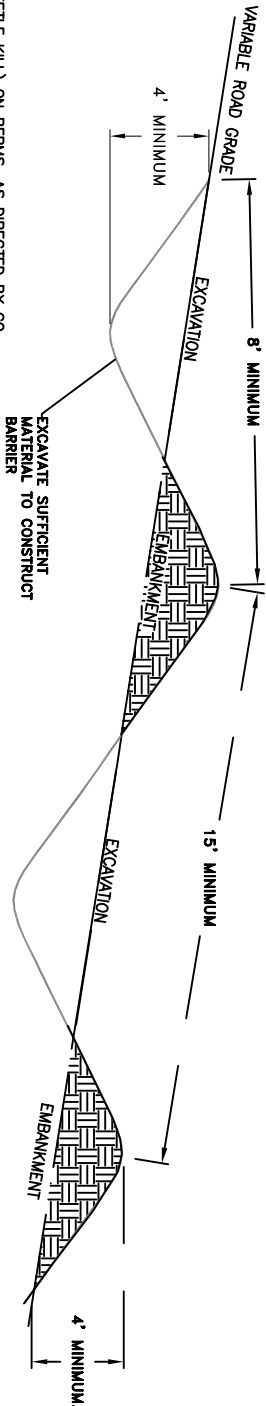

PROFILE VIEW

NOTES


1. SCATTER SLASH, ROCKS, ADJACENT TREES (BEETLE KILL) ON BERMS, AS DIRECTED BY CO.
2. LEAVE BOTTOM OF DIP AND BERM IN ROUGHED CONDITION TO PROMOTE REVEGETATION.

WATER-BAR DETAIL

NO SCALE

NOTES

1. ALL WATERBARS SHALL BEGIN AT THE INTERSECTION OF THE ROADBED AND CUT SLOPE AND RUN ACROSS THE ENTIRE WIDTH OF THE ROADBED.
2. ALL WATERBARS SHALL HAVE FREE FLOWING OUTLETS.
3. WHEN STAKES ARE USED, THEY SHALL DESIGNATE THE OUTLET LOCATION.
4. WATERBARS SHALL BE SKEWED TO FACILITATE DRAINAGE, 30 TO 60 DEGREE ANGLE FORM ROAD CENTERLINE.
5. WATERBARS LOCATIONS SHALL BE STAKED ON THE GROUND OR DIRECTED BY CO.

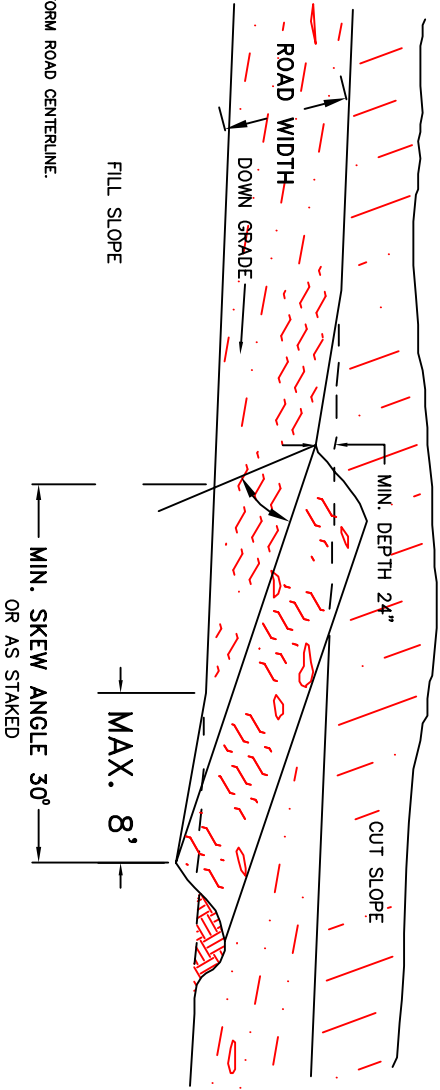

U.S. DEPARTMENT OF AGRICULTURE
FOREST SERVICE
R-2
ROCKY MOUNTAIN REGION

Drawn
Checked
Reviewed


Forest
Project Name
Road Decommissioning

Sheet Title
Waterbar Details/Large Berms

Scale
Not to Scale
Sheet 4
of 6

ROAD ENTRANCE CLOSURE and SMALL EARTH BERM DETAILS


Not to Scale

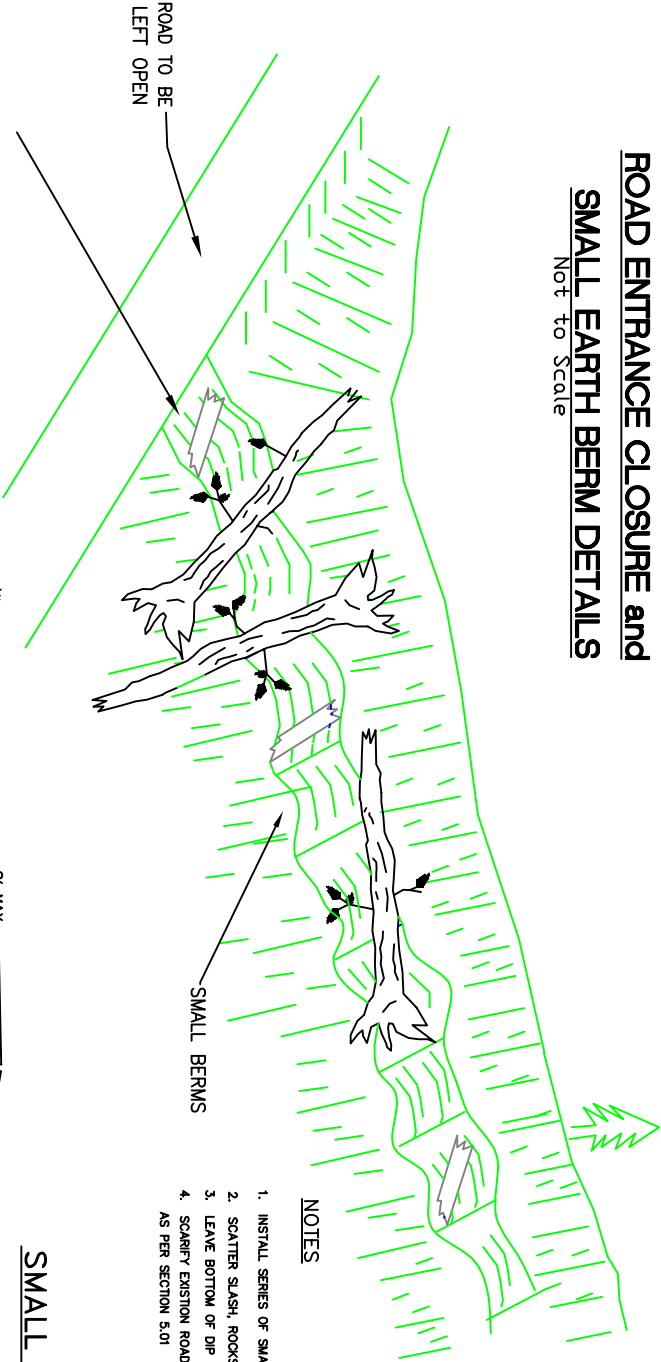

NOTES

1. INSTALL SERIES OF SMALL BERMS AS STAKED ON THE GROUND OR AS DIRECTED BY CO.
2. SCATTER SLASH, ROCKS, ADJACENT TREES (BEETLE KILL) ON SMALL BERMS, AS DIRECTED BY CO.
3. LEAVE BOTTOM OF DIP AND BERM IN ROUGHED CONDITION TO PROMOTE REVEGETATION.
4. SCARIFY EXISTION ROADBED PRIOR TO CONSTRUCTING SMALL BERM, AS PER SECTION 5.01

SMALL BERM DETAIL

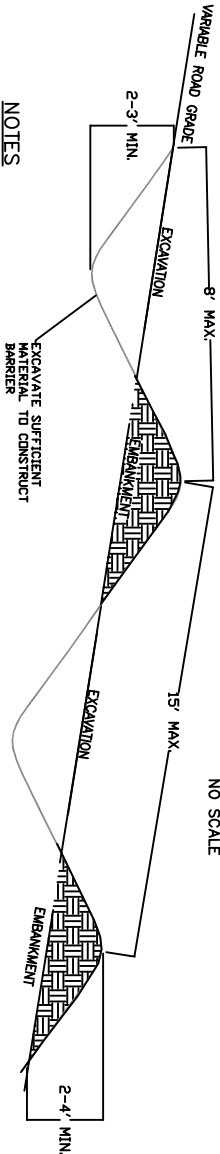

NOTES

1. SCATTER SLASH, ROCKS, ADJACENT TREES (BEETLE KILL) ON SMALL BERMS, AS DIRECTED BY CO.
2. LEAVE BOTTOM OF DIP AND BERM IN ROUGHED CONDITION TO PROMOTE REVEGETATION.

PROFILE VIEW

SMALL EARTH BERMS



U.S. DEPARTMENT OF AGRICULTURE
FOREST SERVICE
R-2
BOCOTY MOUNTAIN REGION

Drawn cliback

Design

Checked

Reviewed

Forest

MEDICINE BOW/ROUTT N.F.


Project Name

ROAD DECOMMISSIONING

Sheet Title

Scale
NOT TO SCALE


Sheet 5
of 6

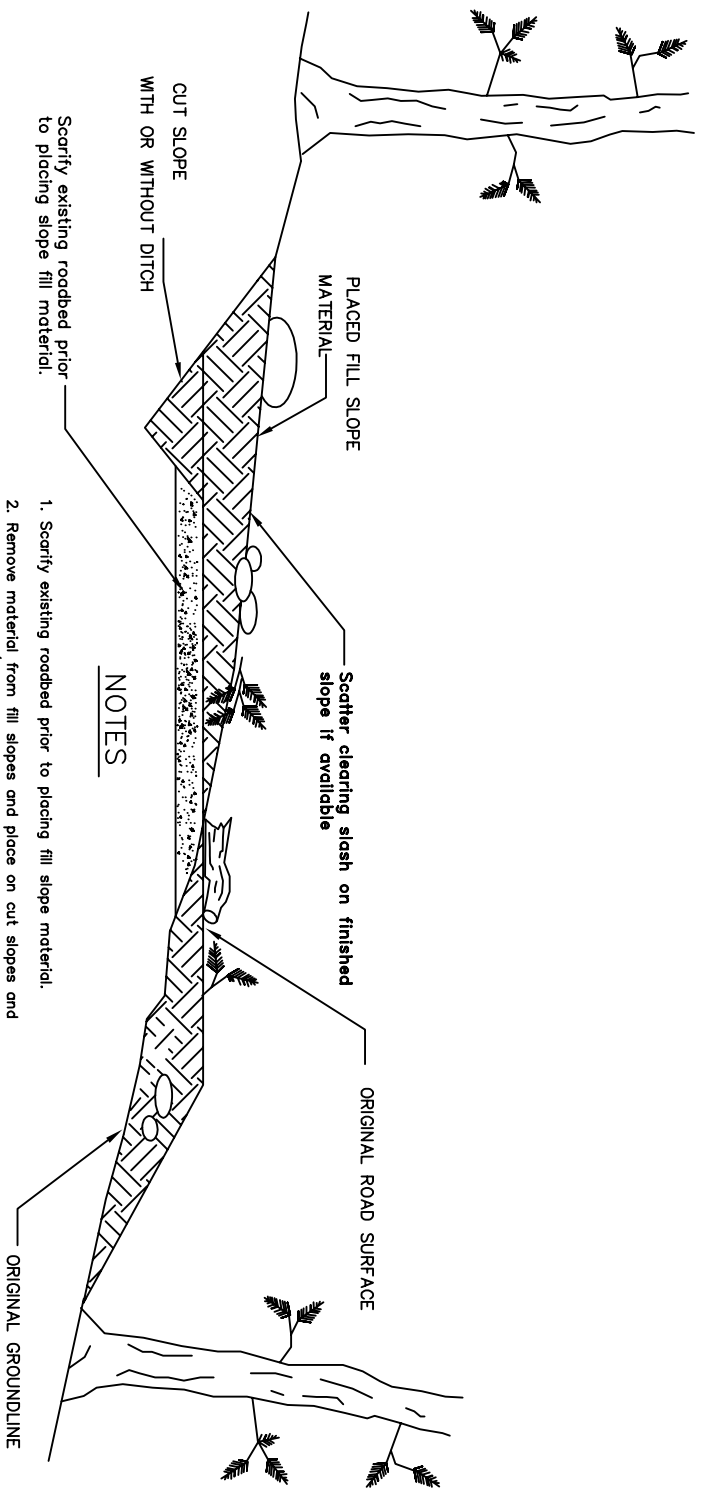

NOTES


1. Scarf existing roadbed prior to placing fill slope material.
2. Remove material from fill slopes and place on cut slopes and shape to a 1 1/2:1 slope or flatter.
3. Place log, rocks, or other materials on disturbed areas to match the natural surroundings.
4. Remove all vegetation from the roadbed prior to recontouring. Scatter removed vegetation on recontoured surface.

Recontour Detail

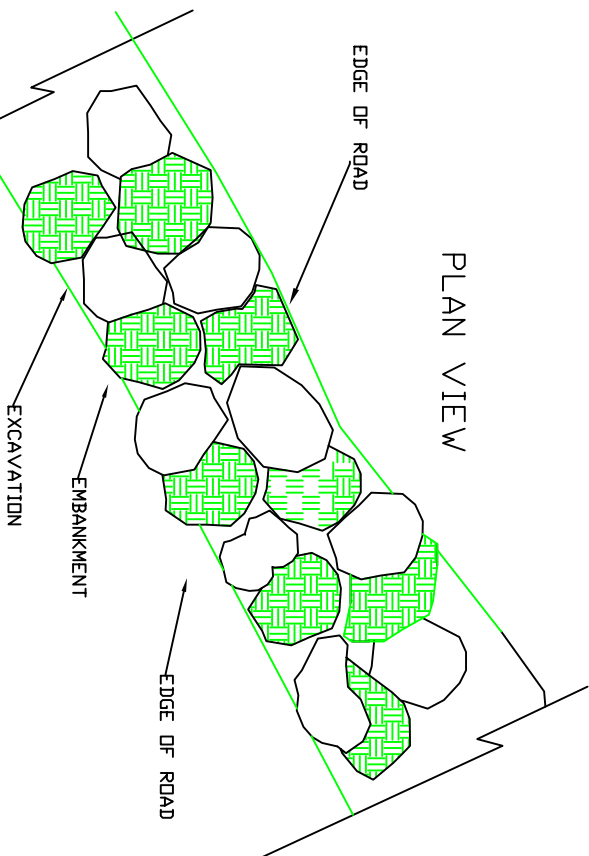

PLAN VIEW

- 1) MOGALS ARE RANDOM DIVITS IN THE GROUND AND ARE TYPICALLY CONSTRUCTED WITH A BACKHOE OR EXCAVATOR.
- 2) EXCAVATED MATERIAL IS PLACED ADJACENT TO DIVOTS.
- 3) PLACE LOGS AND ROCKS, OR OTHER MATERIALS ON DECOMMISSIONED ROADBED TO PREVENT MOTORIZED USE.
- 4) EXCAVATED MATERIAL SHALL BE PLACED ON DECOMPACTED ROAD SURFACE.

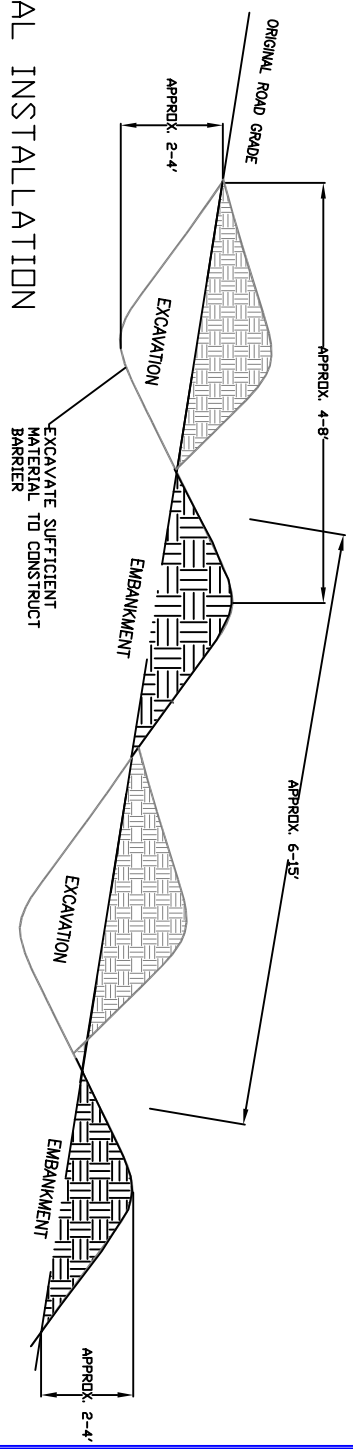

PROFILE VIEW

TYPICAL MOGAL INSTALLATION