
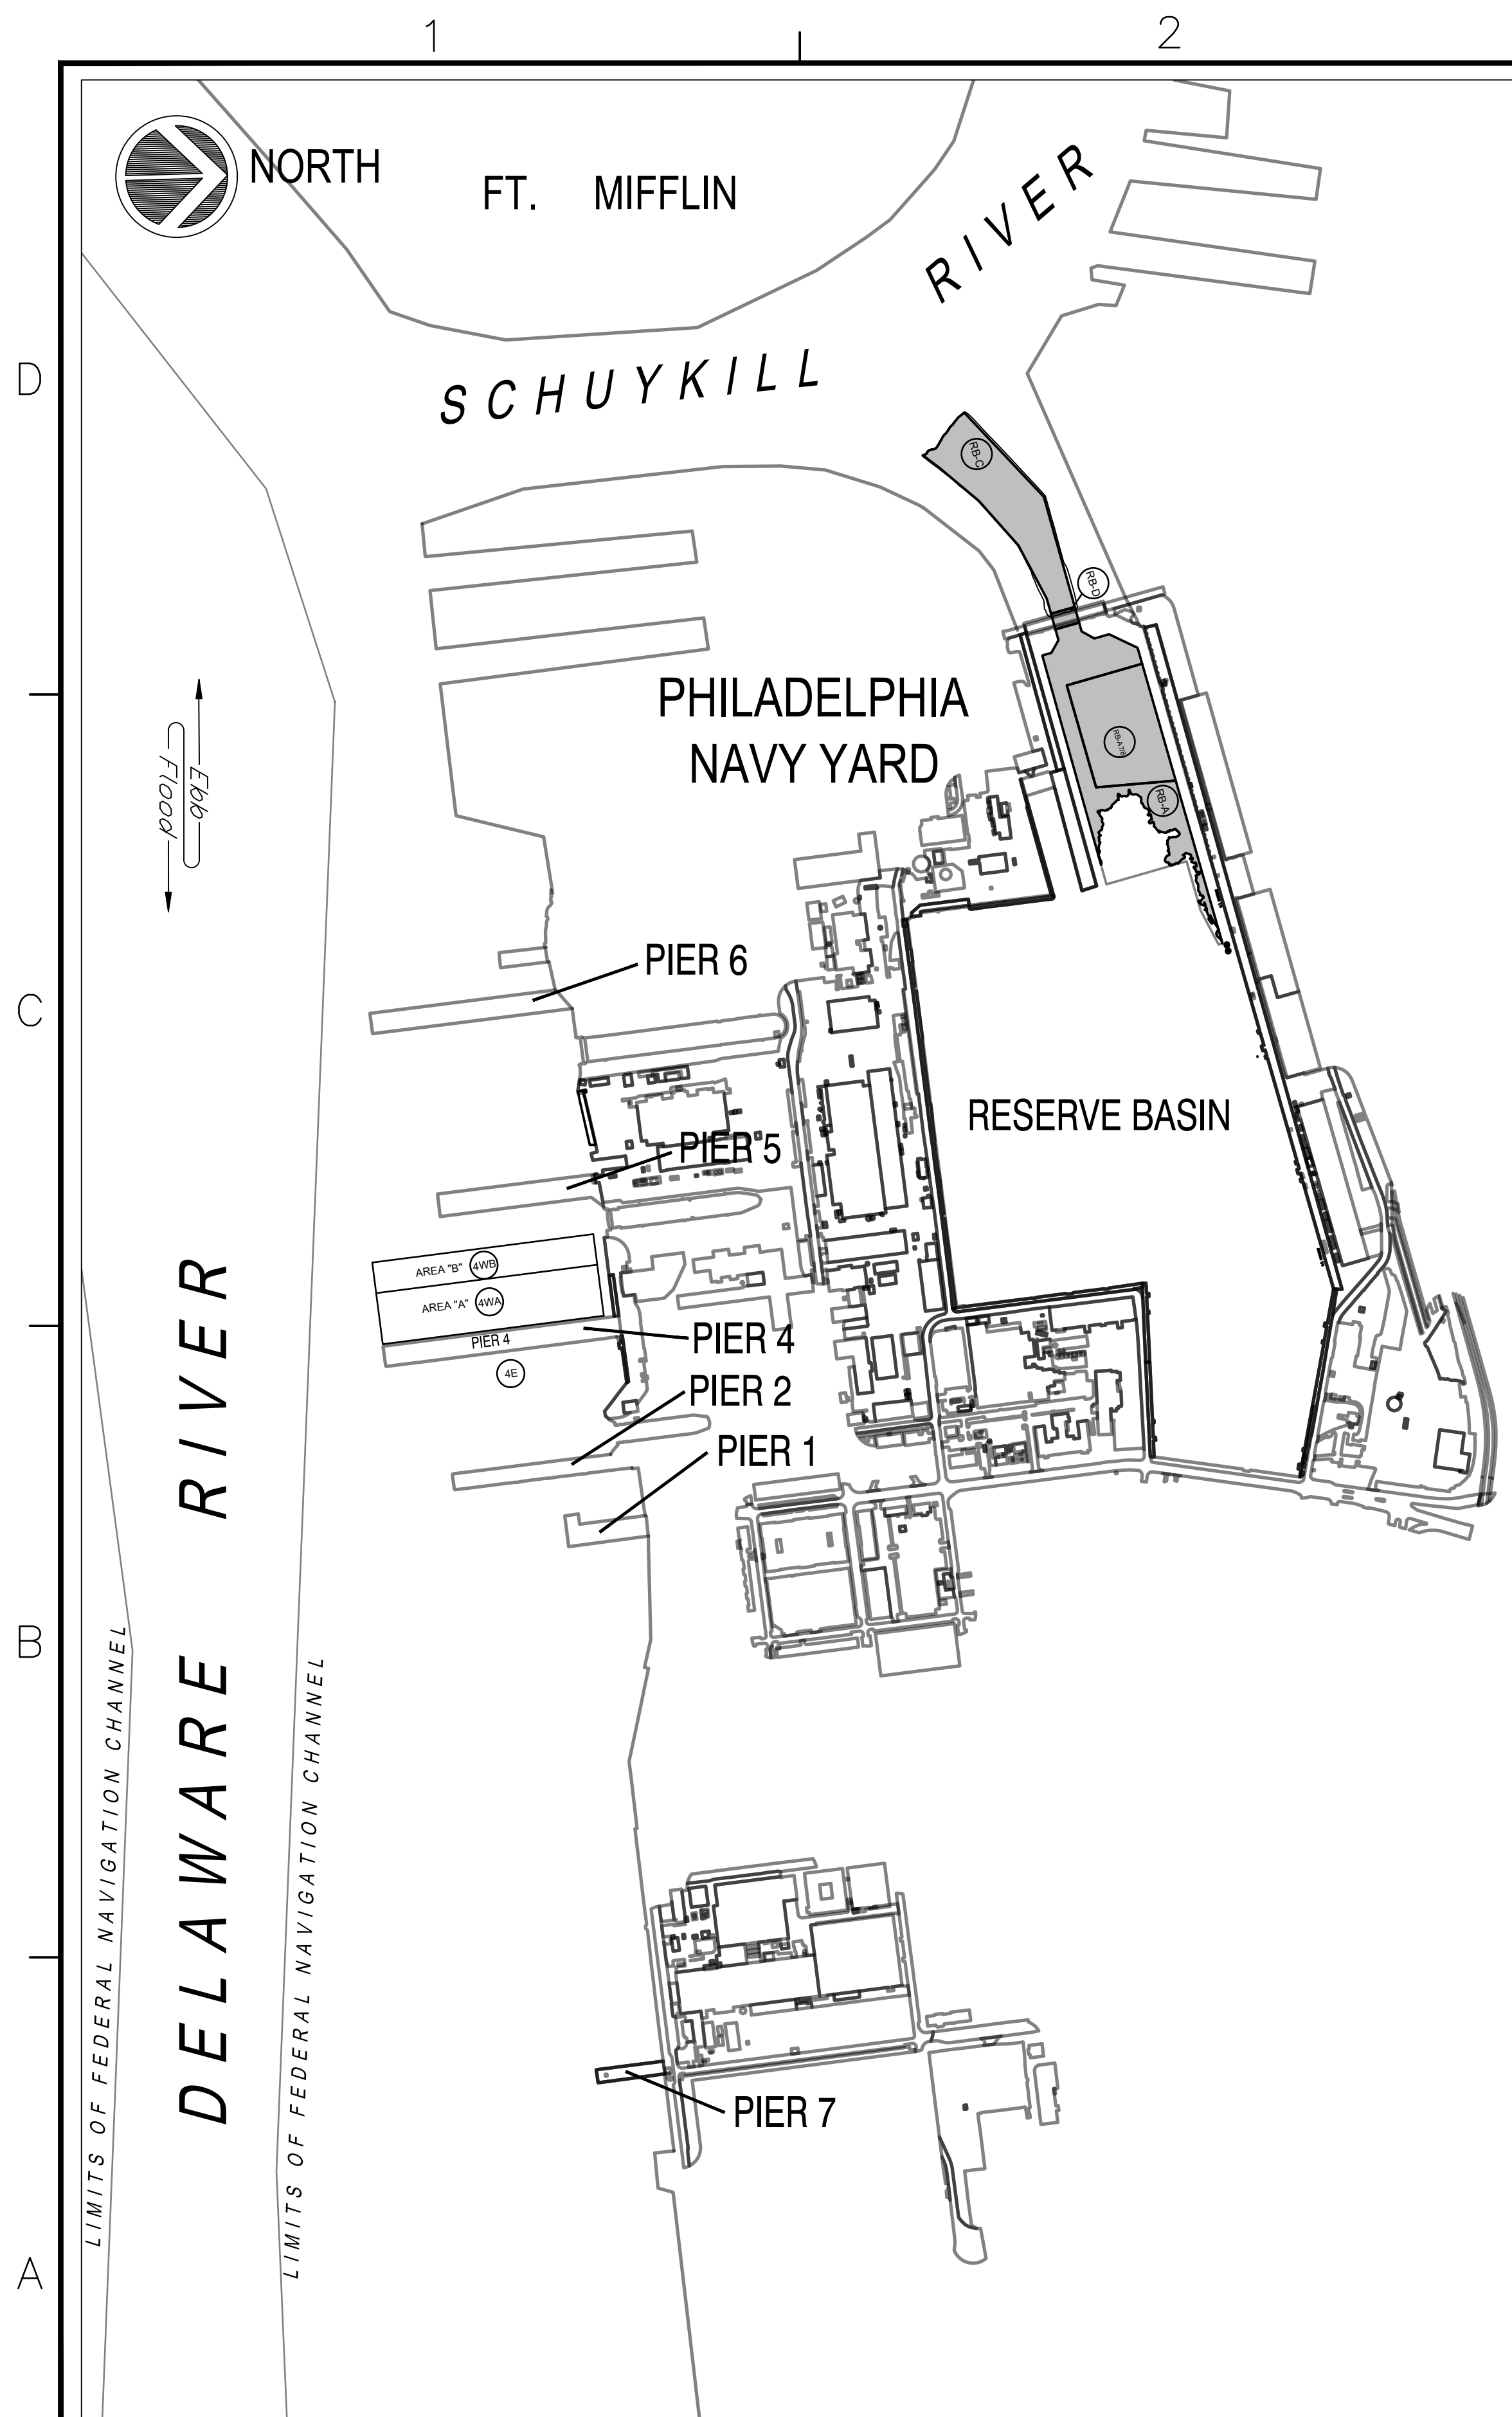


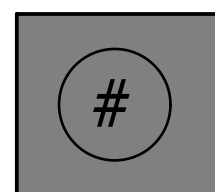

KEY PLAN: INSET 'A'

SCALE: 1" = 600'

## DREDGE AREA LABELS

DREDGE  
AREA ID

BASE BID

SITE PLAN FOR:  
FY 2026 MAINTENANCE DREDGING of RESERVE BASIN  
PHILADELPHIA NAVY YARD - PHILADELPHIA, PA

## LIST OF SHEETS

| SHEET NO. | NAVFAC # | SHEET TITLE           |
|-----------|----------|-----------------------|
| 1. V-001  | 12902788 | TITLE SHEET           |
| 2. V-002  | 12902789 | DETAIL SHEET          |
| 3. V-101  | 12902790 | RESERVE BASIN - SOUTH |

## HYDROGRAPHIC NOTES

1. VERTICAL DATUM - SOUNDINGS ARE IN FEET AND TENTHS AND ARE REFERRED TO THE NOAA MEAN LOWER LOW WATER DATUM (MLLW).
2. THE HYDROGRAPHIC SURVEY WAS CONDUCTED USING CLASS 1 HYDROGRAPHIC SURVEY METHODS & ACCURACIES OUTLINED IN THE CORPS OF ENGINEERS' HYDROGRAPHIC SURVEYING MANUAL (EM 1110-2-1003).
3. ALL BATHYMETRY WAS RECORDED USING A RESON T-50-P MULTI-BEAM SONAR SYSTEM(S) WITH HORIZONTAL POSITIONS OBTAINED VIA APPLANIX POS/MV GPS W/MRU.
4. HORIZONTAL DATUM IS BASED ON THE PENNSYLVANIA SOUTH (LAMBERT) STATE PLANE COORDINATE SYSTEM, ZONE 3702, U.S. SURVEY FEET (NAD 1983).
5. SOUNDING DATA FOR DISPLAY HAS BEEN PROCESSED USING HYPACK/HYSWEEP SOFTWARE AS FOLLOWS: CELL SIZE: 20' X 20', SOUNDING POSITION: CENTER OF CELL, CELL STATISTICS: AVERAGE DEPTH.
6. SOUNDING DATA FOR VOLUME CALCULATIONS HAS BEEN PROCESSED USING HYPACK/HYSWEEP SOFTWARE AS FOLLOWS: CELL SIZE: 5' X 5'; SOUNDING POSITION: CENTER OF CELL, CELL STATISTICS: AVERAGE DEPTH.
7. DREDGING WORK SHALL BE PERFORMED VIA SEALED ENVIRONMENTAL CLAMSHELL BUCKET. IF HARD MATERIAL IS ENCOUNTERED OR DEBRIS REMOVAL IS REQUIRED THEN AND STANDARD CLAMSHELL BUCKET MAY BE UTILIZED. ONCE HARD MATERIAL AND/OR DEBRIS HAS BEEN REMOVED THE CONTRACTOR SHALL SWITCH BACK TO USING THE SEALED ENVIRONMENTAL CLAMSHELL BUCKET.



## LOCATION MAP

NOT TO SCALE



This project was designed by NAVFAC MIDLANT HYDROGRAPHIC BRANCH (PDC 45C) of the Naval Facilities Engineering Systems Command. The initials or signatures and registration designations of individuals appear on these project documents within the scope of their employment as required by NAVFACINST 3540.1E.


[illegible]







FILE NAME: D:\J5000\_Current\_Projects\1783178\_PNY Reserve Basin FY26 Maintenance Dredging\CAD\PNY Reserve Basin FY26 Maintenance Dredging.dwg LAYOUT NAME: V-101 RESERVE BASIN - SOUTH PLOTTED: Tuesday, November 04, 2025 - 12:48pm USER: jgao

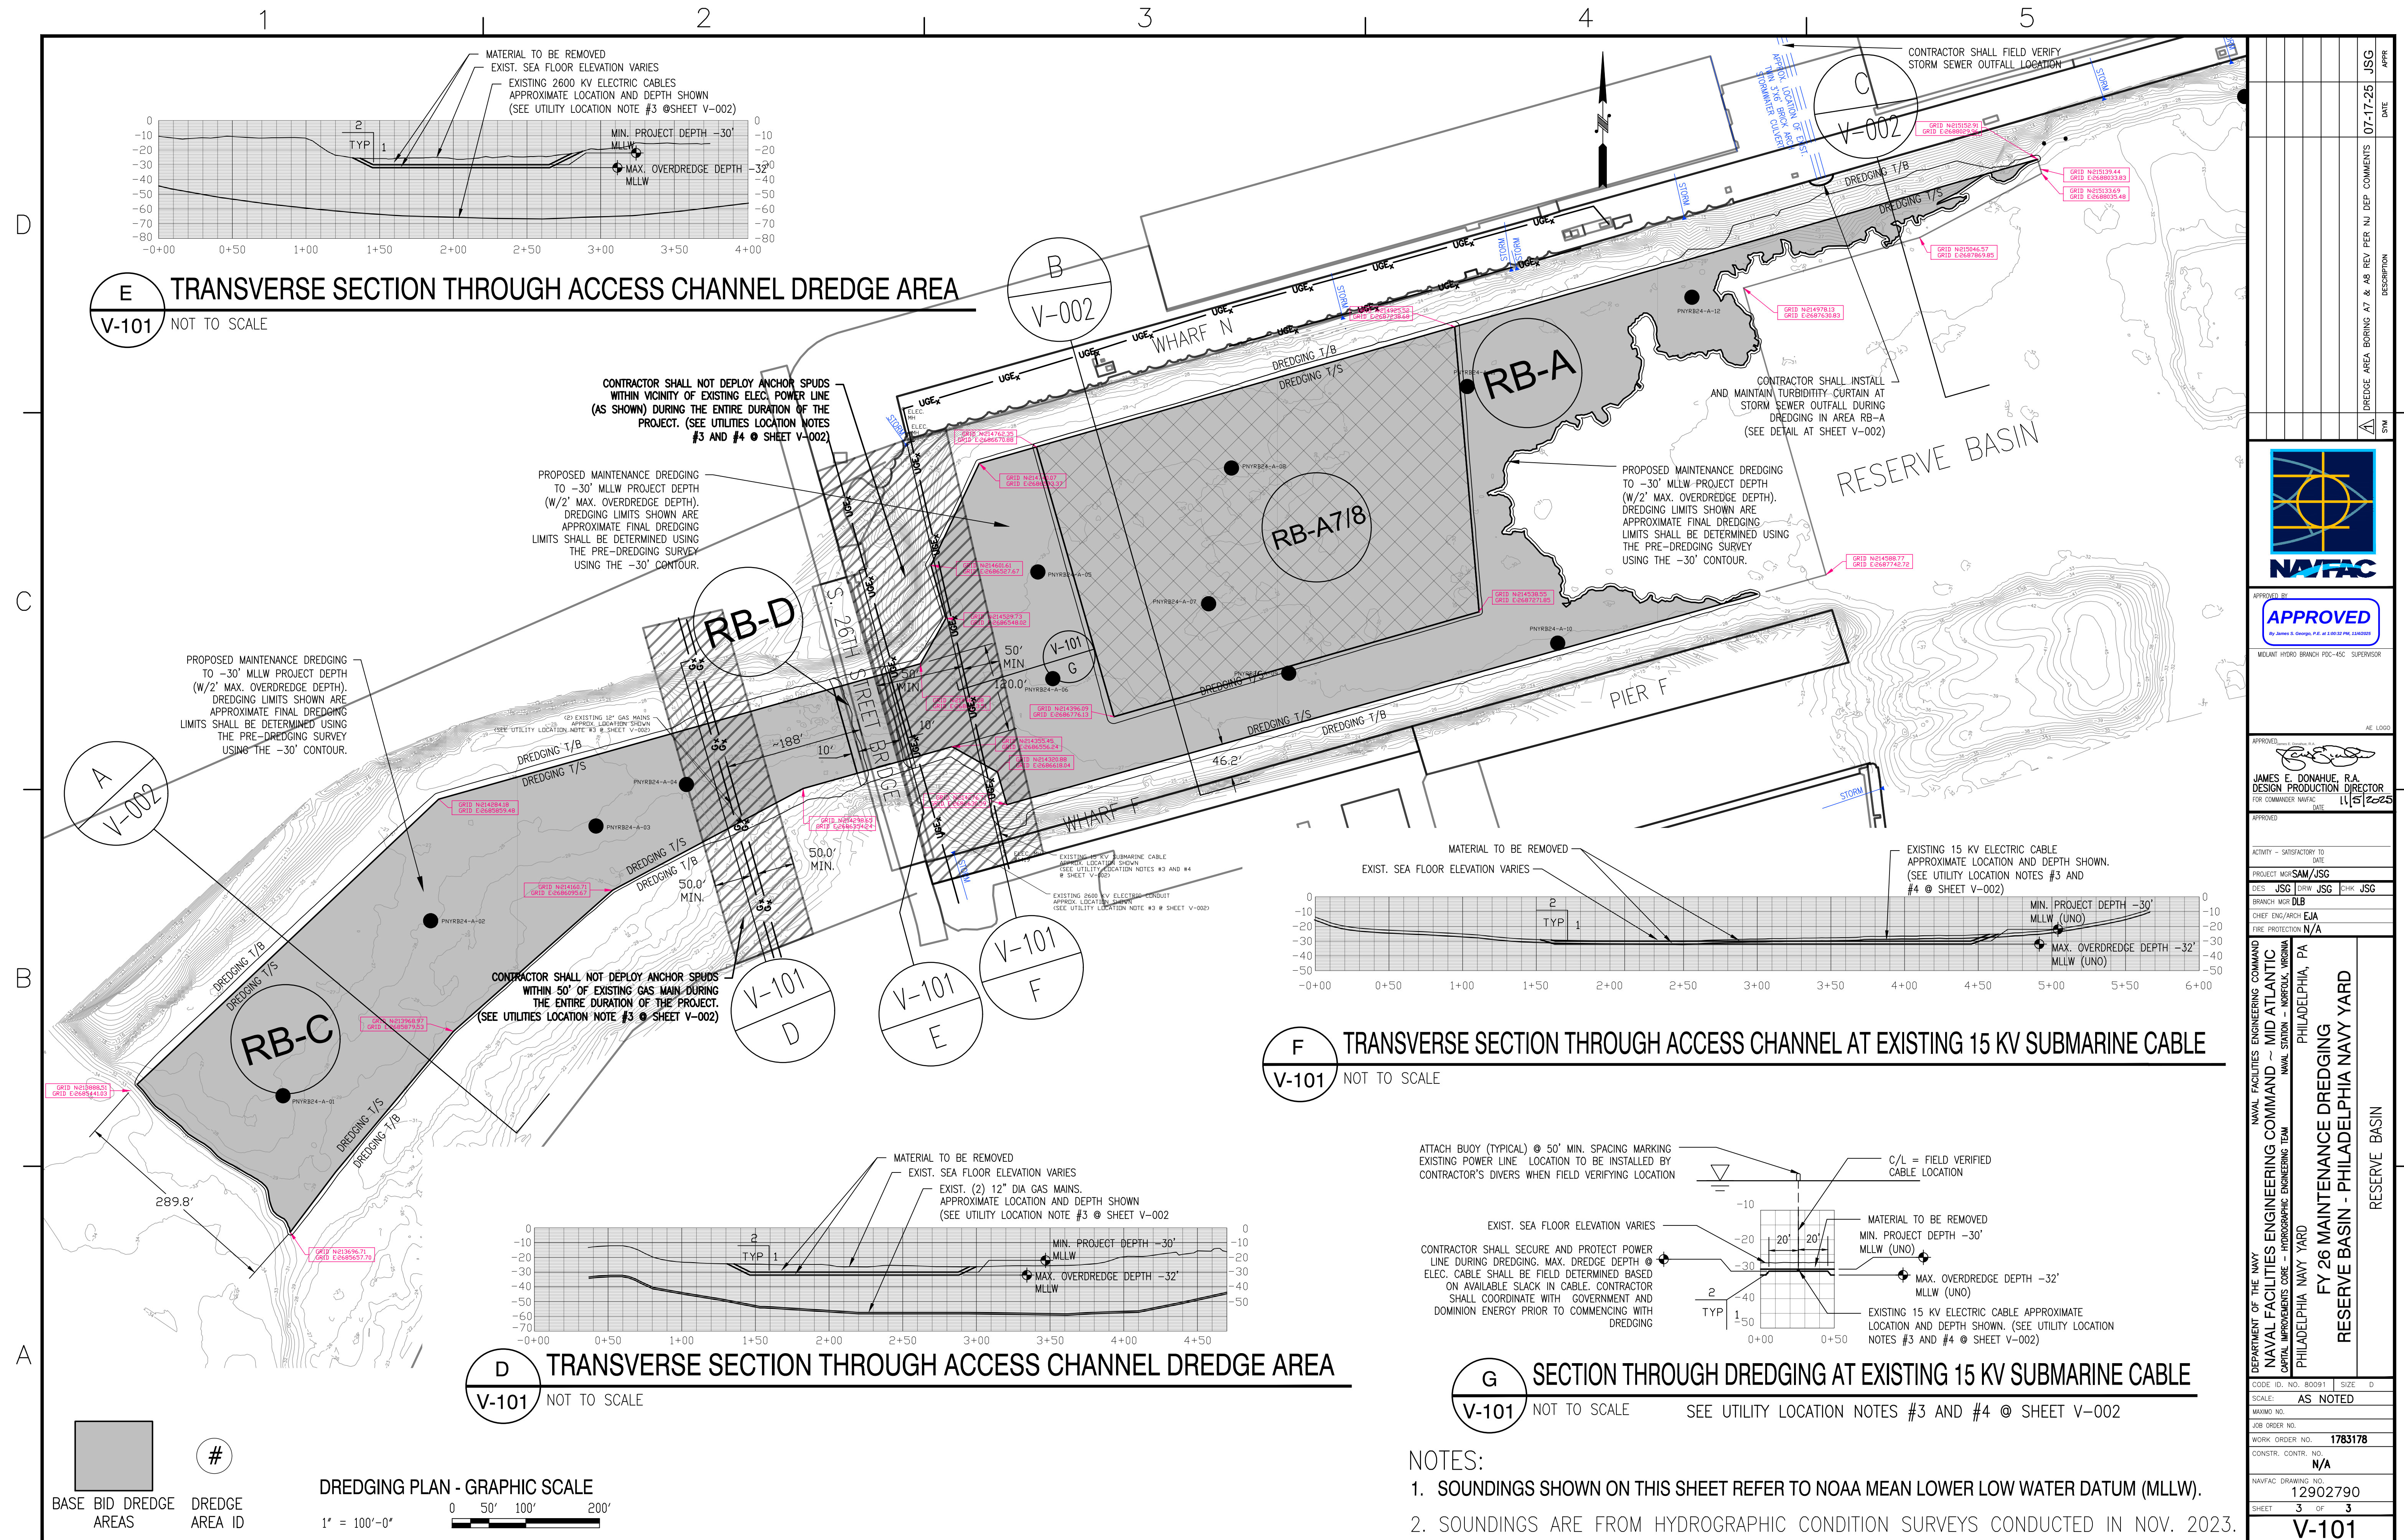

|   |  |                                                                                       |     |
|---|--|---------------------------------------------------------------------------------------|-----|
| DATE   |  | 07-17-25                                                                              | JSG |
| DESCRIPTION   |  | DREDGE AREA BORING A7 & A8 REV PER NJ DEF COMMENTS                                    |     |
| SYM   |  | APR                                                                                   |     |
|   |  |                                                                                       |     |
| APPROVED BY<br><br><b>JAMES E. DONAHUE, R.A.</b><br>DESIGN PRODUCTION DIRECTOR<br>FOR COMMANDER NAVAL<br>DATE 11/5/25                             |  |                                                                                       |     |
| APPROVED<br>ACTIVITY - SATISFACTORY TO DATE<br>PROJECT MGR: SAM/JSG<br>DES: JSG<br>BRANCH MGR: DLB<br>CHIEF ENG/ARCH: EJA<br>FIRE PROTECTION: N/A |  |                                                                                       |     |
| NAVAL FACILITIES ENGINEERING COMMAND<br>CAPITAL IMPROVEMENTS CORE - HYDROGRAPHIC ENGINEERING TEAM<br>PHILADELPHIA NAVY YARD<br>PHILADELPHIA, PA   |  | FY 26 MAINTENANCE DREDGING<br>RESERVE BASIN - PHILADELPHIA NAVY YARD<br>RESERVE BASIN |     |
| CODE ID: NO. 80091   |  | SIZE: D                                                                               |     |
| SCALE: AS NOTED   |  |                                                                                       |     |
| MAXIMO NO.   |  |                                                                                       |     |
| JOB ORDER NO.   |  |                                                                                       |     |
| WORK ORDER NO.   |  | 1783178                                                                               |     |
| CONSTR. CONTR. NO.   |  | N/A                                                                                   |     |
| NAVFAC DRAWING NO.   |  | 12902790                                                                              |     |
| SHEET 3 OF 3   |  | V-101                                                                                 |     |
| DRAWN/REVISED 08-29-18   |  |                                                                                       |     |