




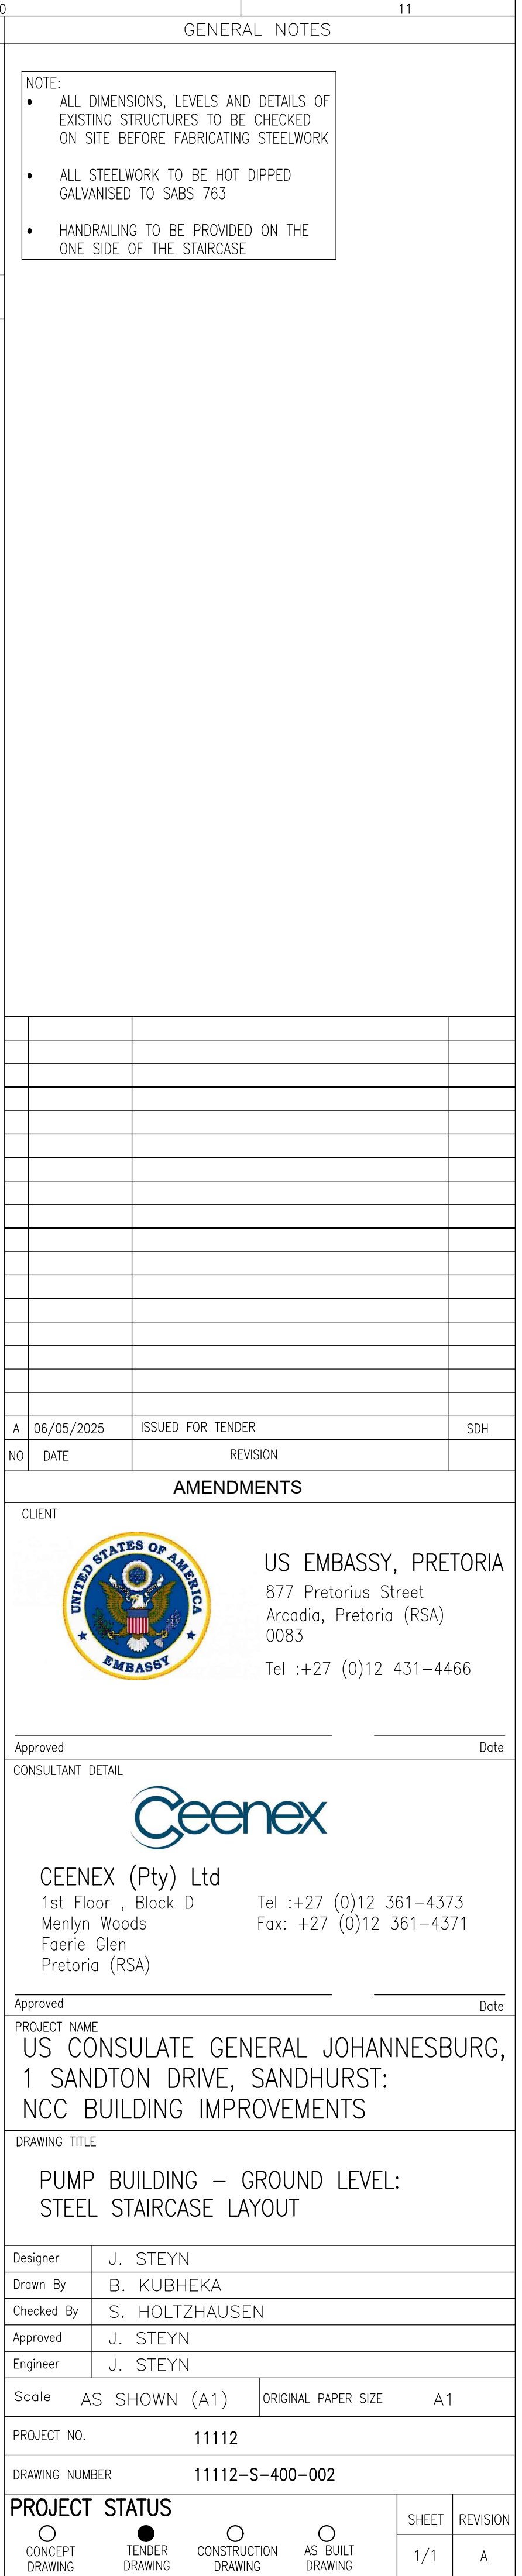


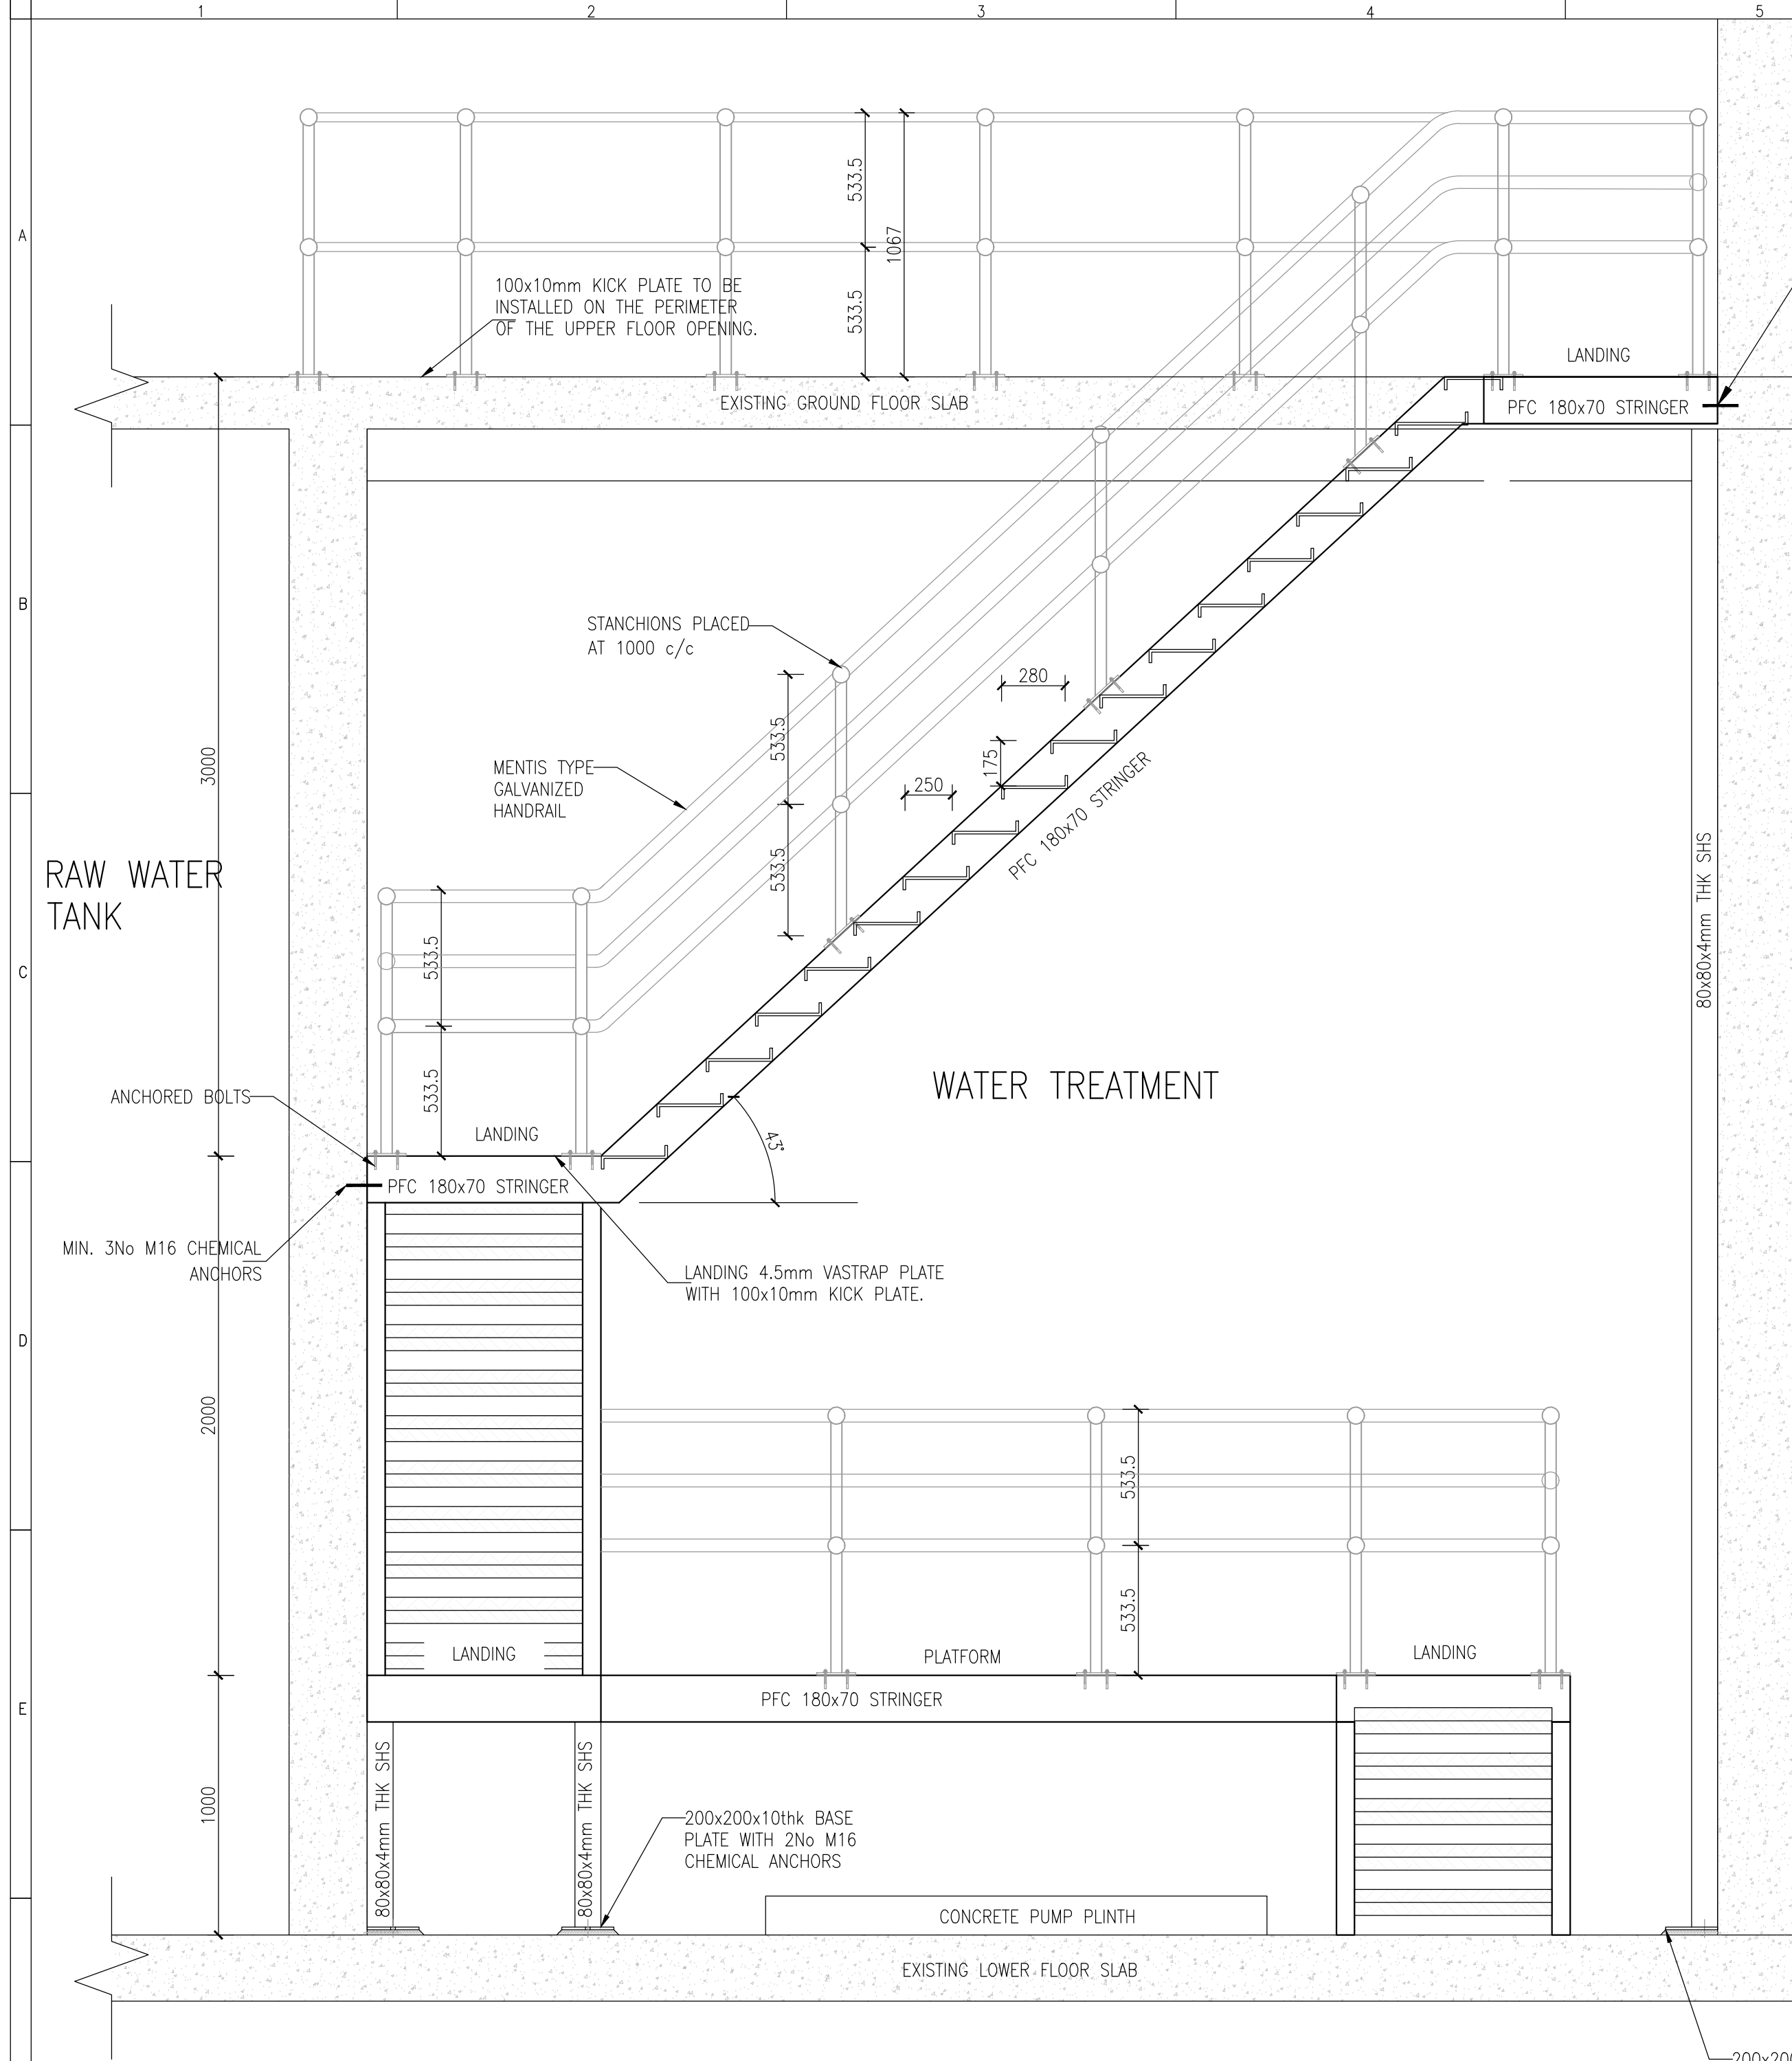


SECTION A-A
SCALE 1:20

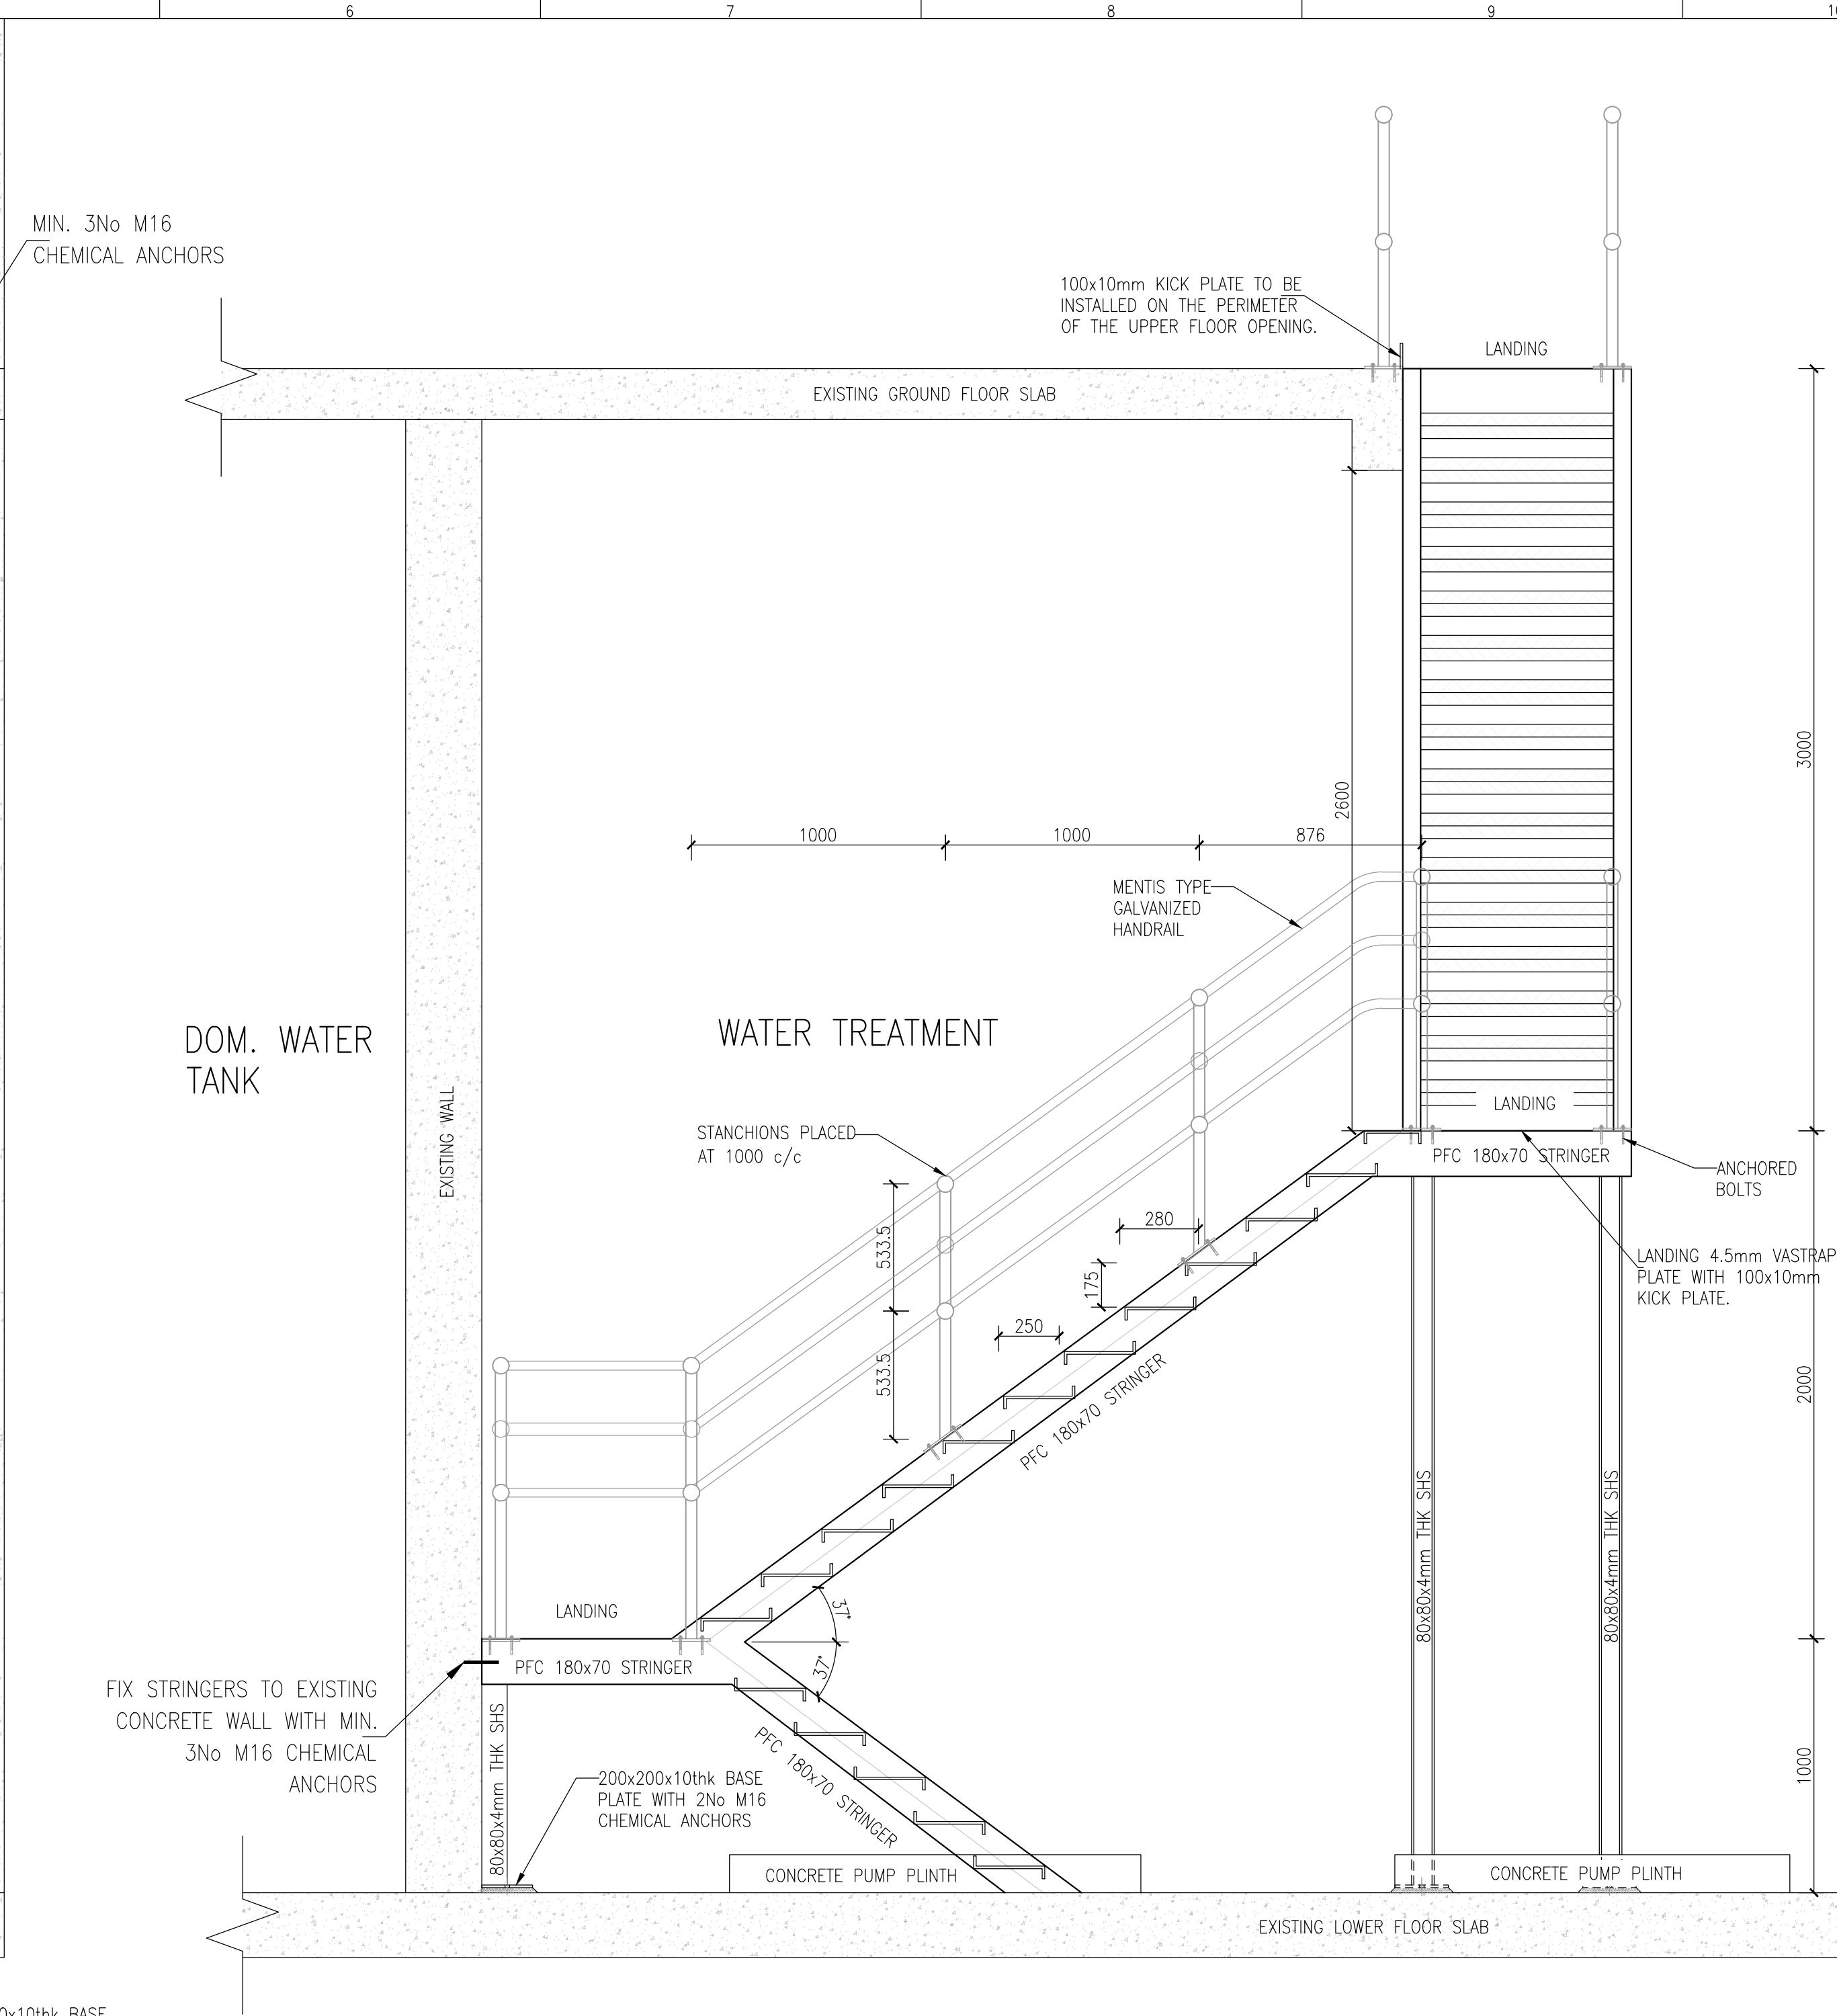


SECTION B-B
SCALE 1:20

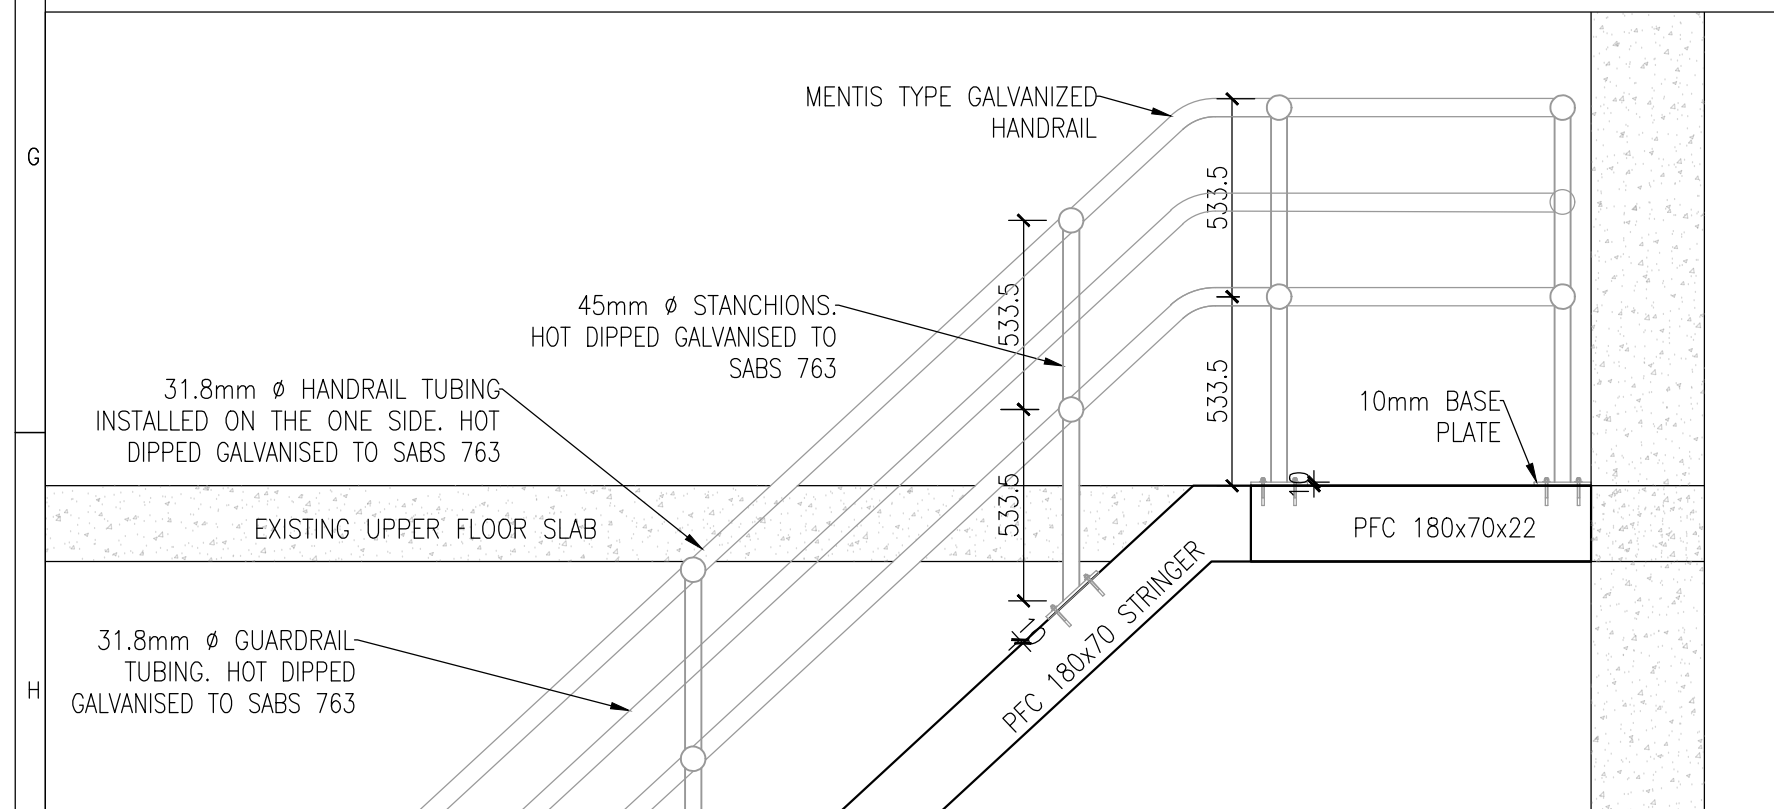

HANDRAIL DETAIL
SCALE 1:20

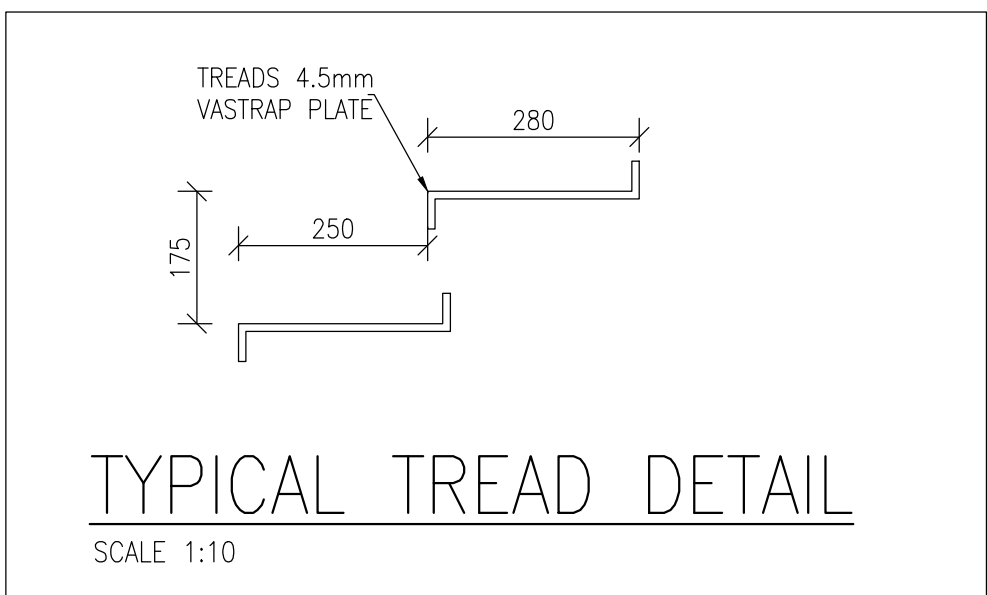

TYPICAL TREAD DETAIL
SCALE 1:10

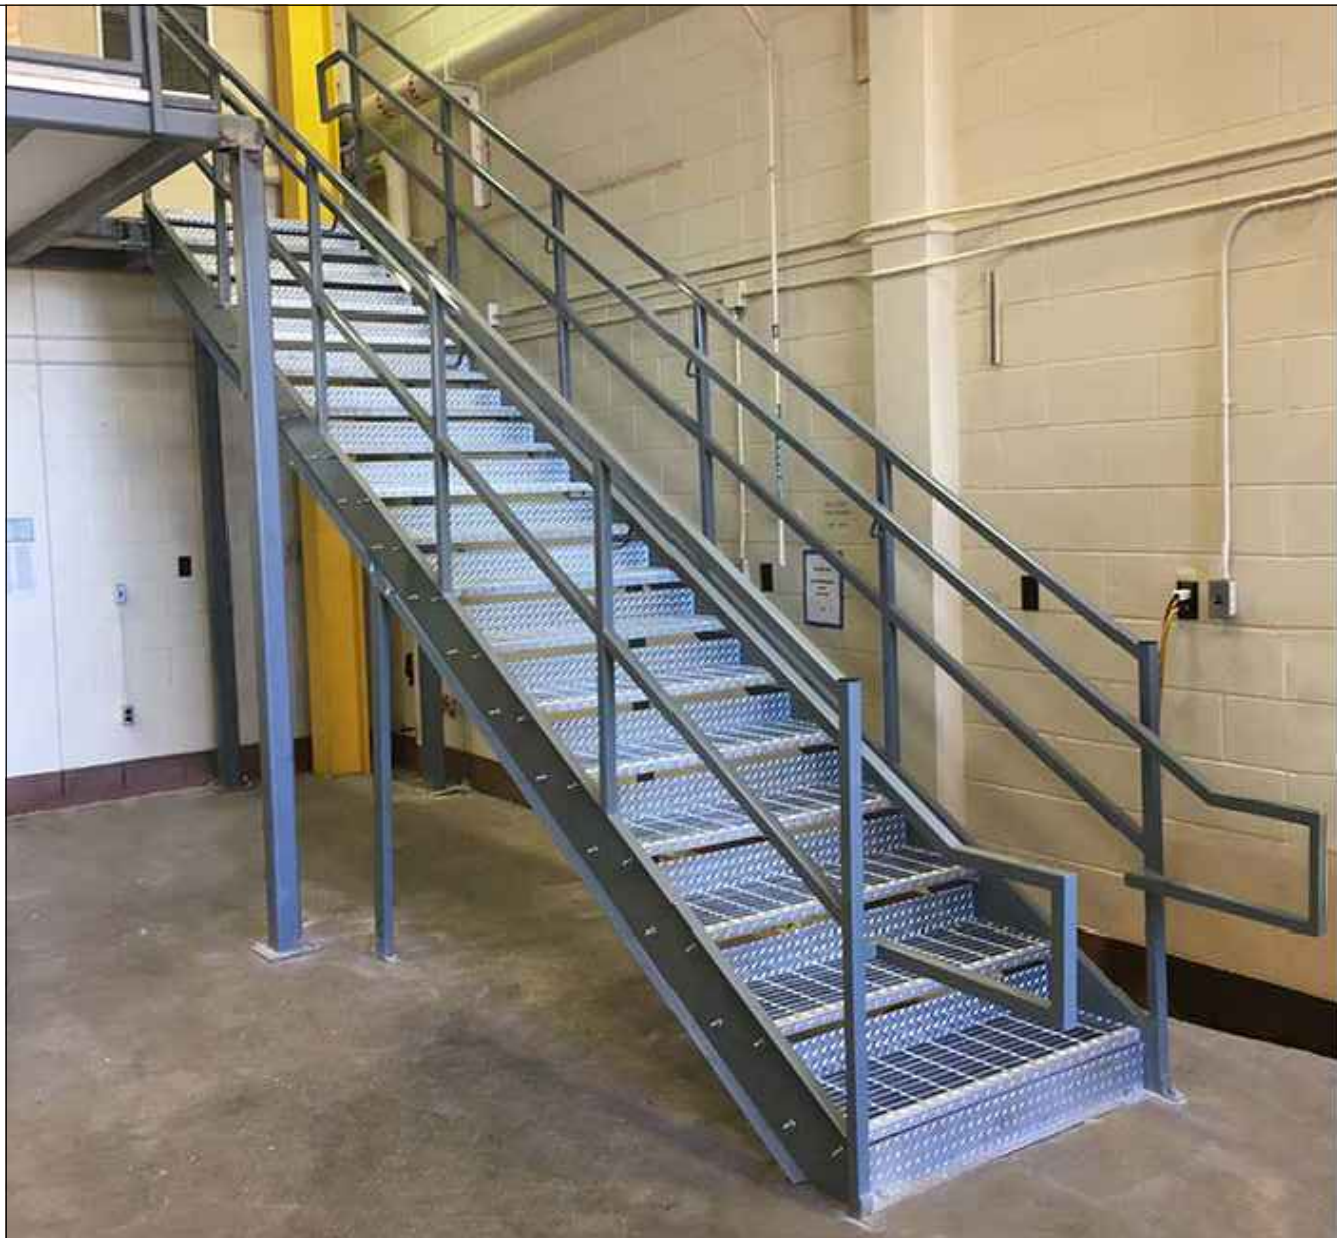

TYPICAL GUARDRAILS WITH HANDRAIL
SCALE 1:20

TENDER DRAWING
UNCLASSIFIED

GENERAL NOTES

- ALL DIMENSIONS, LEVELS AND DETAILS OF EXISTING STRUCTURES TO BE CHECKED ON SITE BEFORE FABRICATING STEELWORK
- ALL STEELWORK TO BE HOT DIPPED GALVANISED TO SABS 763
- HANDRAILING TO BE PROVIDED ON THE ONE SIDE OF THE STAIRCASE

NO	DATE	REVISION	SDH
A	06/05/2025	ISSUED FOR TENDER	SDH

AMENDMENTS

CLIENT

US EMBASSY, PRETORIA
877 Pretorius Street
Arcadia, Pretoria (RSA)
0083
Tel :+27 (0)12 431-4466

Approved _____ Date _____

CONSULTANT DETAIL

CEENEX (Pty) Ltd
1st Floor , Block D
Menlyn Woods
Faerie Glen
Pretoria (RSA)

Tel :+27 (0)12 361-4373
Fax: +27 (0)12 361-4371

Approved _____ Date _____

PROJECT NAME
US CONSULATE GENERAL JOHANNESBURG,
1 SANDTON DRIVE, SANDHURST:
NCC BUILDING IMPROVEMENTS

DRAWING TITLE
PUMP BUILDING:
STEEL STAIRCASE SECTIONS AND DETAILS

Designer	J. STEYN		
Drawn By	B. KUBHEKA		
Checked By	S. HOLTZHAUSEN		
Approved	J. STEYN		
Engineer	J. STEYN		
Scale	AS SHOWN	ORIGINAL PAPER SIZE	A1

PROJECT NO. 11112

DRAWING NUMBER 11112-S-400-003

PROJECT STATUS

CONCEPT DRAWING	TENDER DRAWING	CONSTRUCTION DRAWING	AS BUILT DRAWING	SHEET	REVISION
☐	☒	☐	☐	1/1	A