



GENERAL NOTES


- SEE DRAWINGS BB001 TO BB005 FOR BORING LOG DETAILS.
- ALL DIMENSIONS SHOWN IN CALLOUT/NOTES ARE IN METERS UNLESS OTHERWISE NOTED. PIPE DIMENSIONS ARE IN MILLIMETERS.

SHEET LEGEND

- PROJECT LIMITS
- EXISTING MAJOR CONTOUR
- EXISTING MINOR CONTOUR
- 100 YEAR FLOOD PLAIN
- 500 YEAR FLOOD PLAIN
- EXISTING ELECTRICAL LINE
- EXISTING COMMUNICATION LINE
- EXISTING SEWERLINE
- EXISTING DRAINLINE
- EXISTING WATERLINE
- EXISTING NON POTABLE WATER
- CONTROL POINT
- EXISTING STORM DRAIN MANHOLE
- EXISTING DRAIN INLET
- EXISTING SEWER MANHOLE
- EXISTING WATER VALVE
- EXISTING TREE
- APPROXIMATE LOCATION OF BORINGS

CLIN 0001-0004

KEY PLAN

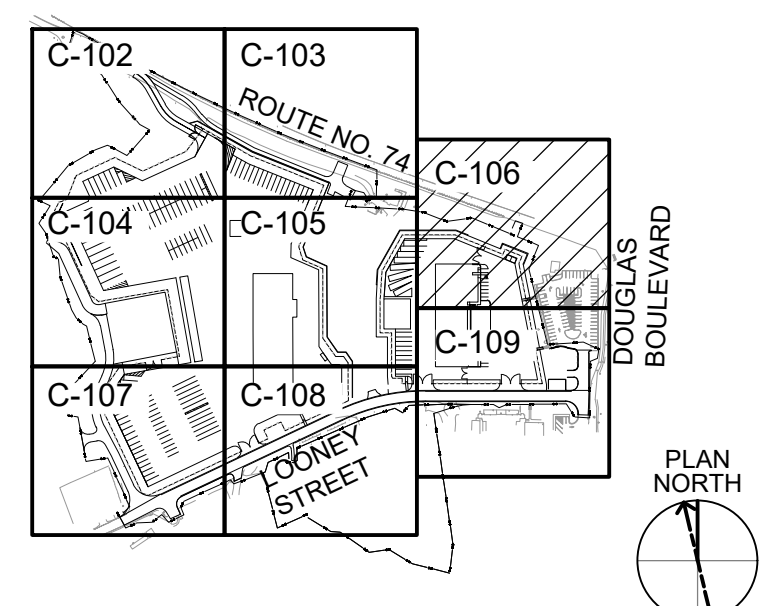

US Army Corps of Engineers®

ISSUE DATE:		SOLICITATION NO.:		CONTRACT NO.:		SCALE:		AS SHOWN		FILE NAME:	
DESIGNED BY:		DRAWN BY:		CHECKED BY:		SUBMITTED BY:		SIZE:		ISO A1	
US ARMY CORPS OF ENGINEERS		JAPAN DISTRICT, OKINAWA AREA OFFICE		USAD-J UNIT 35132		APO, AP 96374-5132		SSM INTERNATIONAL, INC.		501 SUMNER STREET, SUITE 620 HONOLULU, HAWAII 96817	

KADENA AIR BASE, OKINAWA, JAPAN

VEHICLE MAINTENANCE SHOP

FY20 MCA PN77833

EXISTING CONDITION PLAN - 5 (CLIN 0001 - CLIN 0004)

SHEET ID


C-106

INTERMEDIATE DESIGN



GENERAL NOTES

1. SEE DRAWINGS BB001 TO BB005 FOR BORING LOG DETAILS.
2. ALL DIMENSIONS SHOWN IN CALLOUT/NOTES ARE IN METERS UNLESS OTHERWISE NOTED. PIPE DIMENSIONS ARE IN MILLIMETERS.

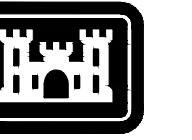


**U.S. Army Corps
Engineers®**

SHEET LEGEND

- | | |
|---|------------------------------------|
|  | PROJECT LIMITS |
|  | EXISTING MAJOR CONTOUR |
|  | EXISTING MINOR CONTOUR |
|  | 100 YEAR FLOOD PLAIN |
|  | 500 YEAR FLOOD PLAIN |
|  | EXISTING ELECTRICAL LINE |
|  | EXISTING COMMUNICATION LINE |
|  | EXISTING SEWERLINE |
|  | EXISTING DRAINLINE |
|  | EXISTING WATERLINE |
|  | EXISTING NON POTABLE WATER |
|  | CONTROL POINT |
|  | EXISTING STORM DRAIN MANHOLE |
|  | EXISTING DRAIN INLET |
|  | EXISTING SEWER MANHOLE |
|  | EXISTING WATER VALVE |
|  | EXISTING TREE |
|  | APPROXIMATE
LOCATION OF BORINGS |

KEY PLAN

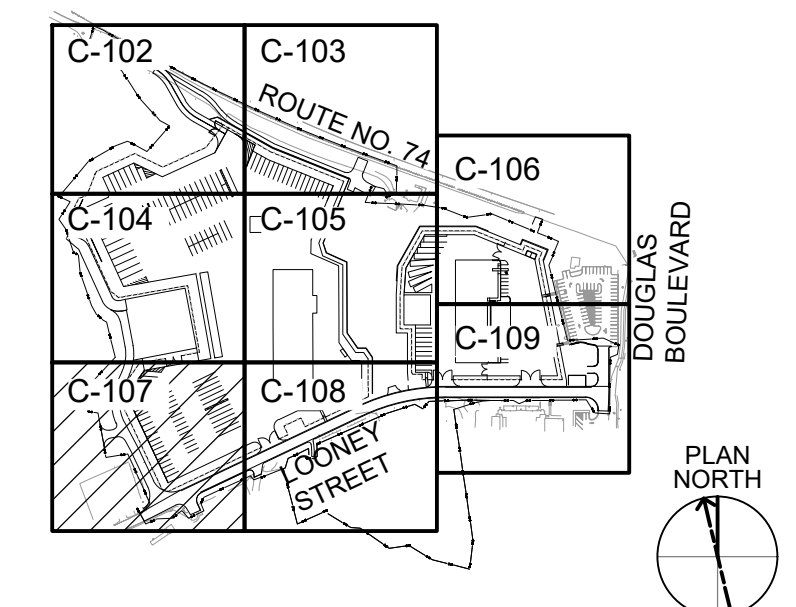

MADEIRA AIR BASE, OKINAWA, JAPAN
VEHICLE MAINTENANCE SHOP
FY20 MCA PN77833

SHEET ID
C-107

INTERMEDIATE DESIGN



A1 EXISTING CONDITION PLAN - 7 (CLIN 0001 - CLIN 0004)
SCALE: 1:250

GENERAL NOTES


- SEE DRAWINGS BB001 TO BB005 FOR BORING LOG DETAILS.
- ALL DIMENSIONS SHOWN IN CALLOUT/NOTES ARE IN METERS UNLESS OTHERWISE NOTED. PIPE DIMENSIONS ARE IN MILLIMETERS.

SHEET LEGEND

- PROJECT LIMITS
- EXISTING MAJOR CONTOUR
- EXISTING MINOR CONTOUR
- 100 YEAR FLOOD PLAIN
- 500 YEAR FLOOD PLAIN
- EXISTING ELECTRICAL LINE
- EXISTING COMMUNICATION LINE
- EXISTING SEWERLINE
- EXISTING DRAINLINE
- EXISTING WATERLINE
- EXISTING NON POTABLE WATER
- CONTROL POINT
- EXISTING STORM DRAIN MANHOLE
- EXISTING DRAIN INLET
- EXISTING SEWER MANHOLE
- EXISTING WATER VALVE
- EXISTING TREE
- APPROXIMATE LOCATION OF BORINGS

CLIN 0001-0004

KEY PLAN

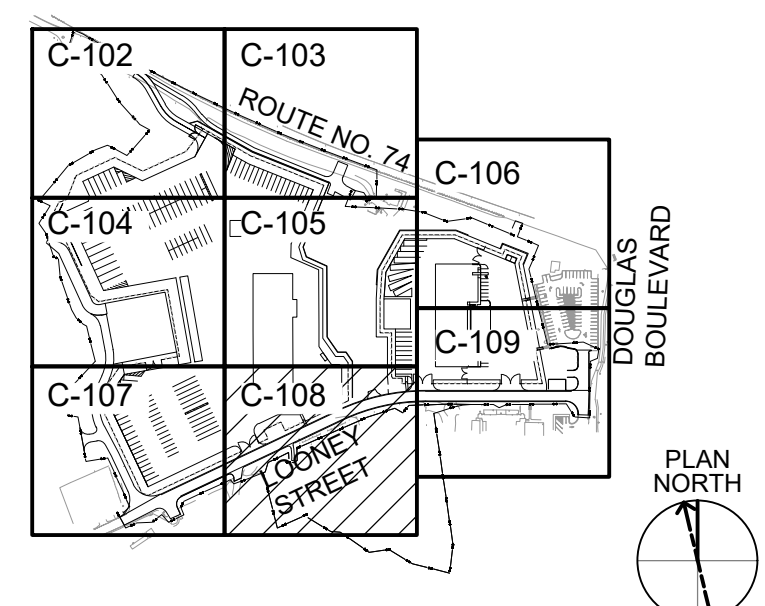

US Army Corps of Engineers®


ISSUE DATE:		SOLICITATION NO.:		CONTRACT NO.:	
DESIGNED BY:	DRAWN BY:	CHECKED BY:	SUBMITTED BY:	SCALE:	AS SHOWN
US ARMY CORPS OF ENGINEERS JAPAN DISTRICT, OKINAWA AREA OFFICE USAD-J, UNIT 35132 APO, AP 96374-5132		SSFM INTERNATIONAL, INC. 501 SUMNER STREET, SUITE 620 HONOLULU, HAWAII 96817		FILE NAME:	ISO A1

KADENA AIR BASE, OKINAWA, JAPAN
VEHICLE MAINTENANCE SHOP
FY20 MCA PN77833

EXISTING CONDITION PLAN - 7 (CLIN 0001 - CLIN 0004)

SHEET ID
C-108

INTERMEDIATE DESIGN

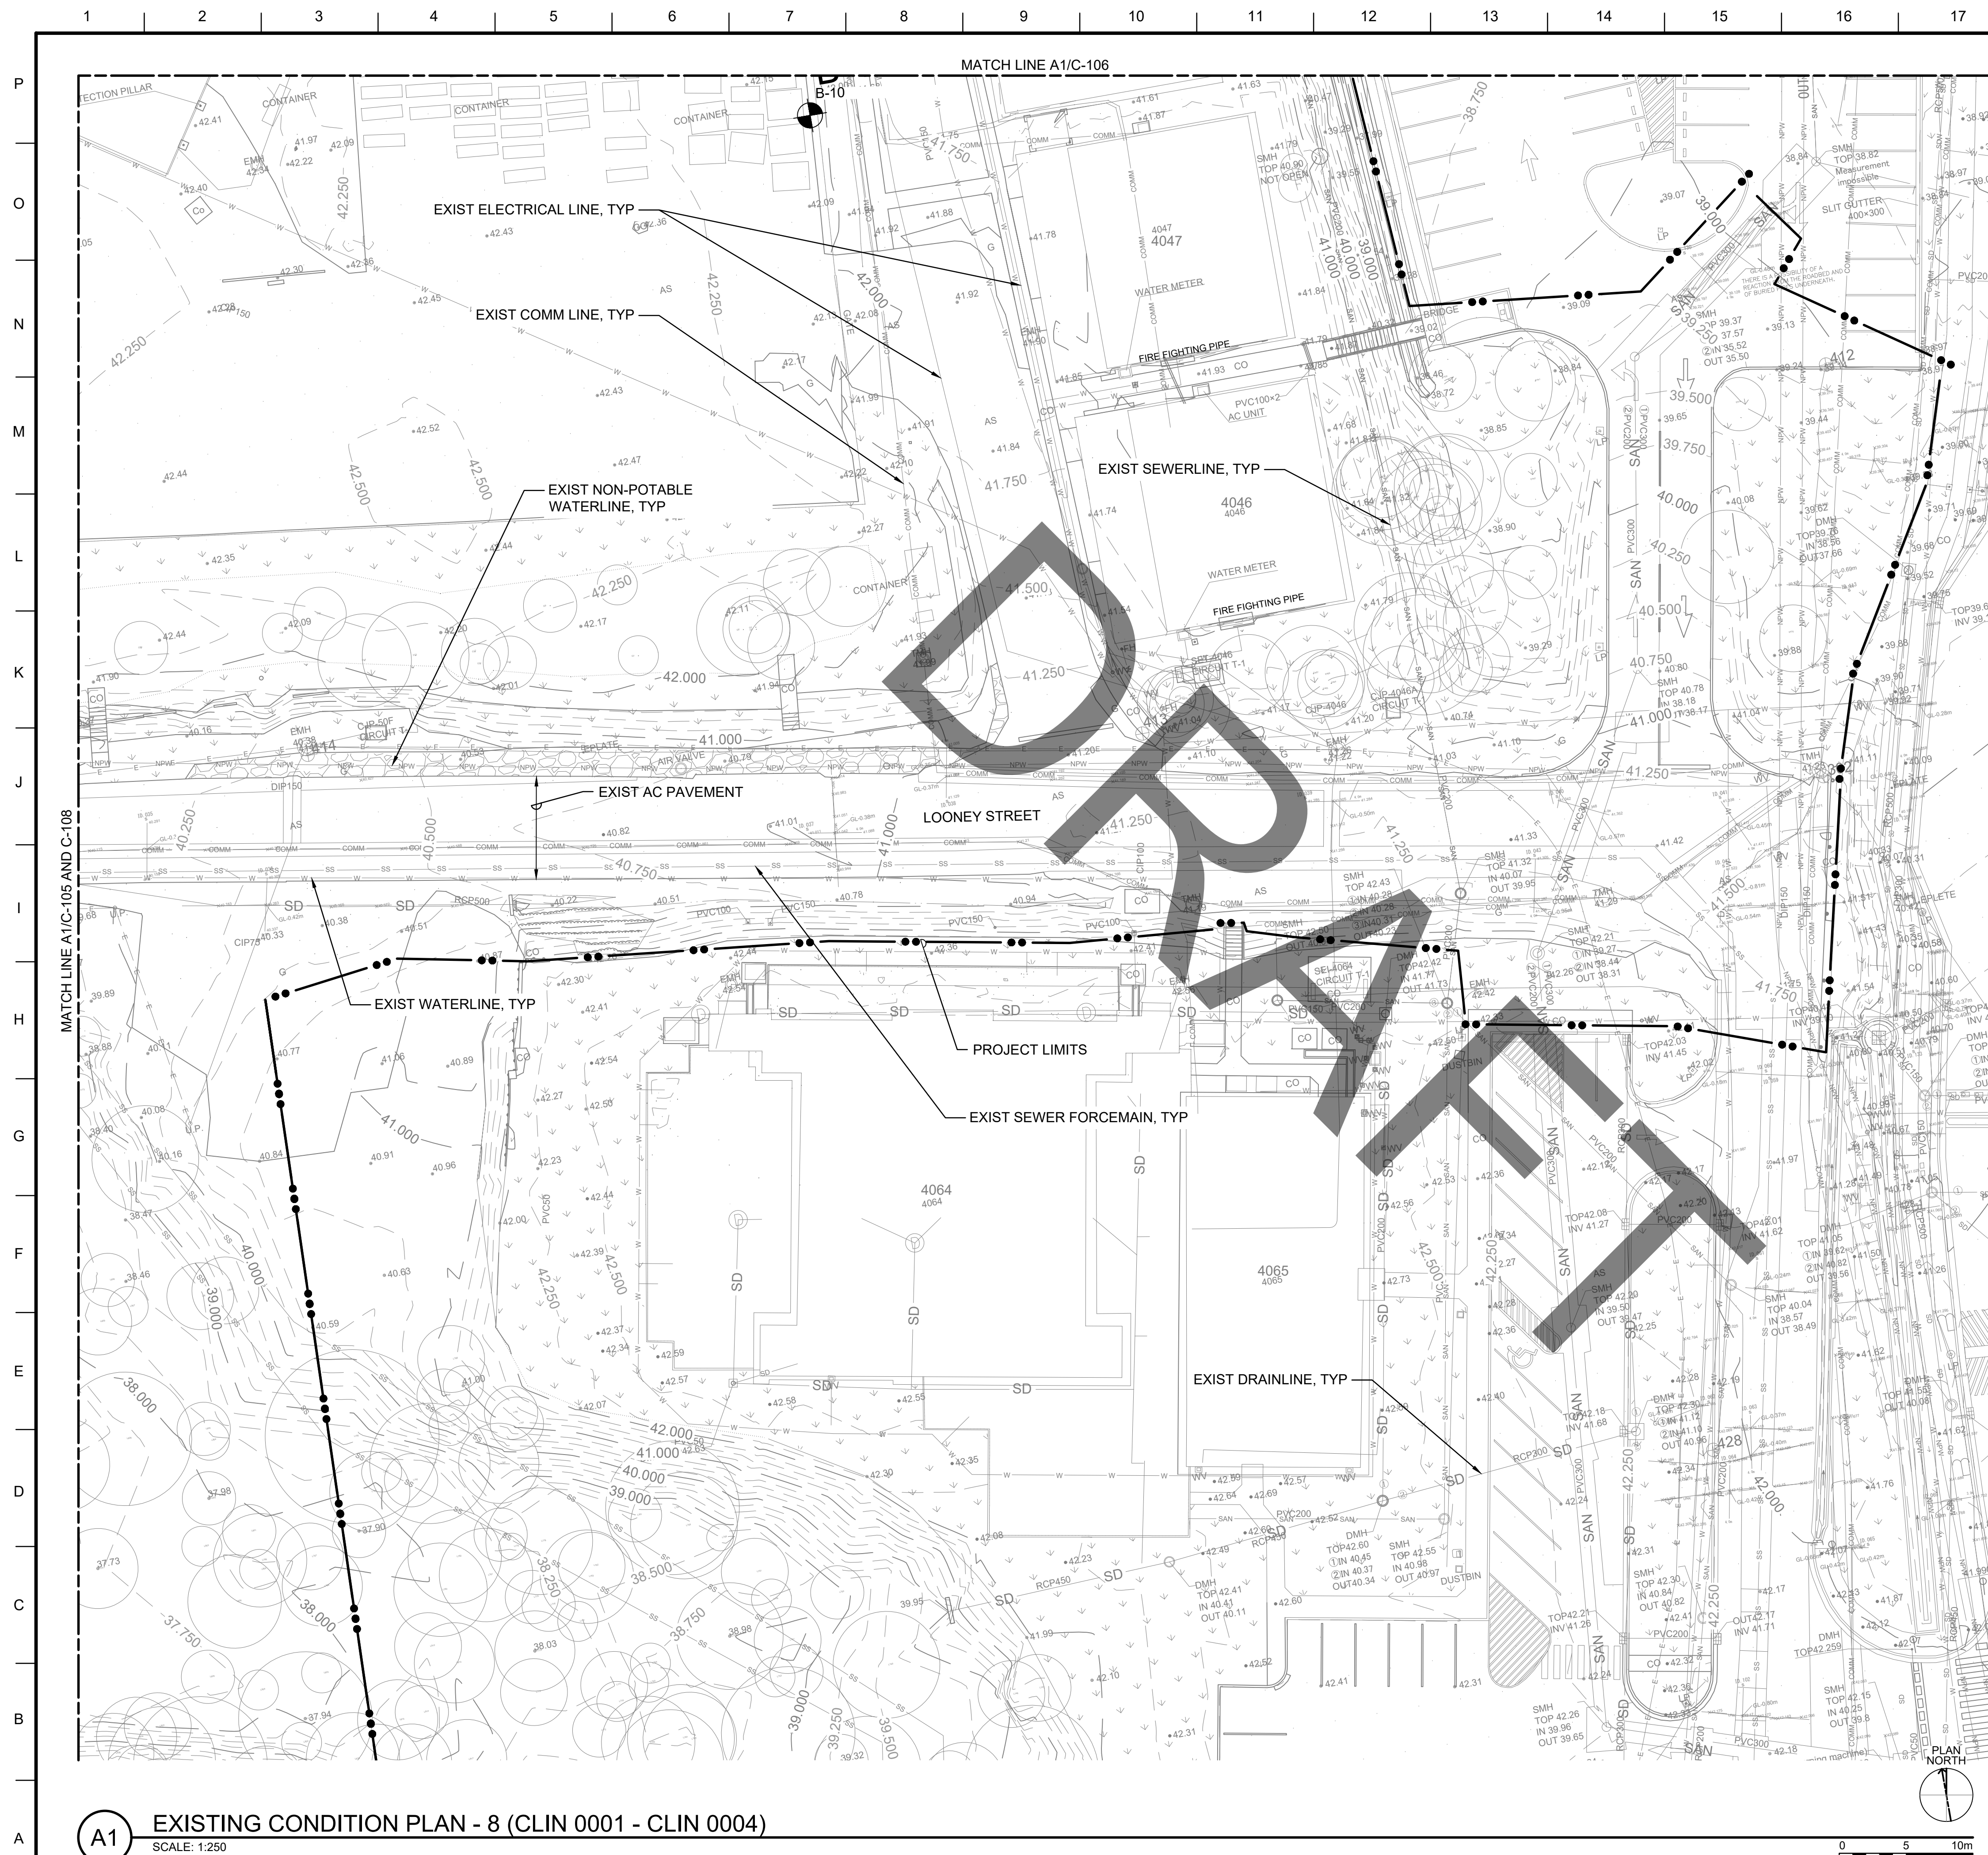

GENERAL NOTES

1. SEE DRAWINGS BB001 TO BB005 FOR BORING LOG DETAILS.
2. ALL DIMENSIONS SHOWN IN CALLOUT/NOTES ARE IN METERS UNLESS OTHERWISE NOTED. PIPE DIMENSIONS ARE IN MILLIMETERS.




**S Army Corps
Engineers®**

SHEET LEGEND

- | | |
|--|------------------------------------|
| | PROJECT LIMITS |
| | EXISTING MAJOR CONTOUR |
| | EXISTING MINOR CONTOUR |
| | 100 YEAR FLOOD PLAIN |
| | 500 YEAR FLOOD PLAIN |
| | EXISTING ELECTRICAL LINE |
| | EXISTING COMMUNICATION LINE |
| | EXISTING SEWERLINE |
| | EXISTING DRAINLINE |
| | EXISTING WATERLINE |
| | EXISTING NON POTABLE WATER |
| | CONTROL POINT |
| | EXISTING STORM DRAIN MANHOLE |
| | EXISTING DRAIN INLET |
| | EXISTING SEWER MANHOLE |
| | EXISTING WATER VALVE |
| | EXISTING TREE |
| | APPROXIMATE
LOCATION OF BORINGS |

KEY PLAN

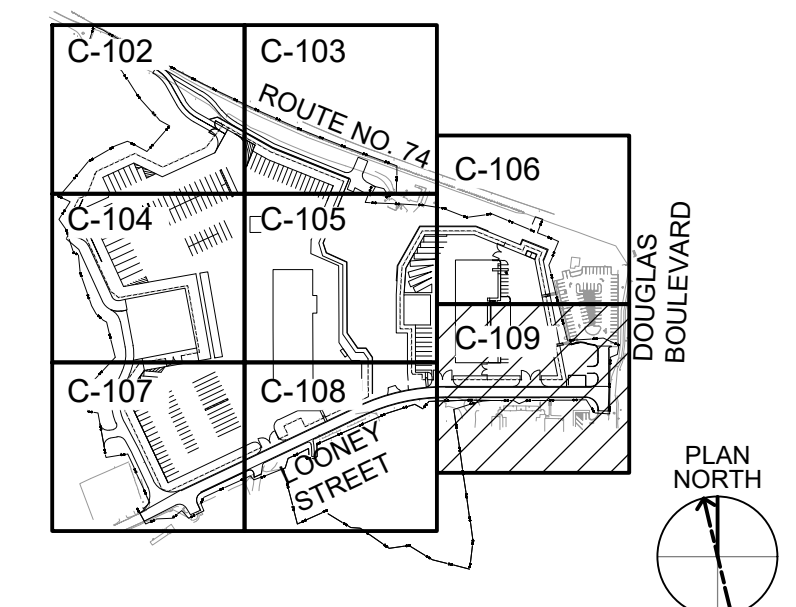

INTERMEDIATE DESIGN

DRAWN BY:	SOLICITATION NO.:
-----------	-------------------

OSAKI CORP. OF ENGINEERS
NAGASAKI DISTRICT, OKINAWA AREA OFFICE

VEHICLE MAINTENANCE SHOP


9

C-109

CONTROL POINT SUMMARY TABLE (BASED ON JGD2011 ZONE 15 DATUM)				
No	MONUMENT TYPE	X	Y	ELEV.
202	BRASS MARKER	39560.492	29029.609	54.443
203	BRASS MARKER	39678.005	29260.554	51.117

GENERAL NOTES

1. ALL DIMENSIONS SHOWN IN CALLOUT/NOTES ARE IN METERS UNLESS OTHERWISE NOTED.

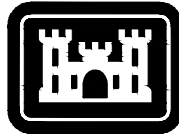


US Army Corps
of Engineers®

SHEET LEGEND

- PROJECT LIMITS
- EXISTING MAJOR CONTOUR
- EXISTING MINOR CONTOUR
- 100 YEAR FLOOD PLAIN
- 500 YEAR FLOOD PLAIN
- EXISTING ELECTRICAL LINE
- EXISTING COMMUNICATION LINE
- EXISTING SEWERLINE
- EXISTING DRAINLINE
- EXISTING WATERLINE
- EXISTING NON POTABLE WATER
- CONTROL POINT
- EXISTING STORM DRAIN MANHOLE
- EXISTING DRAIN INLET
- EXISTING SEWER MANHOLE
- EXISTING WATER VALVE
- EXISTING TREE
- APPROXIMATE LOCATION OF BORINGS

CLIN 0004


KEY PLAN

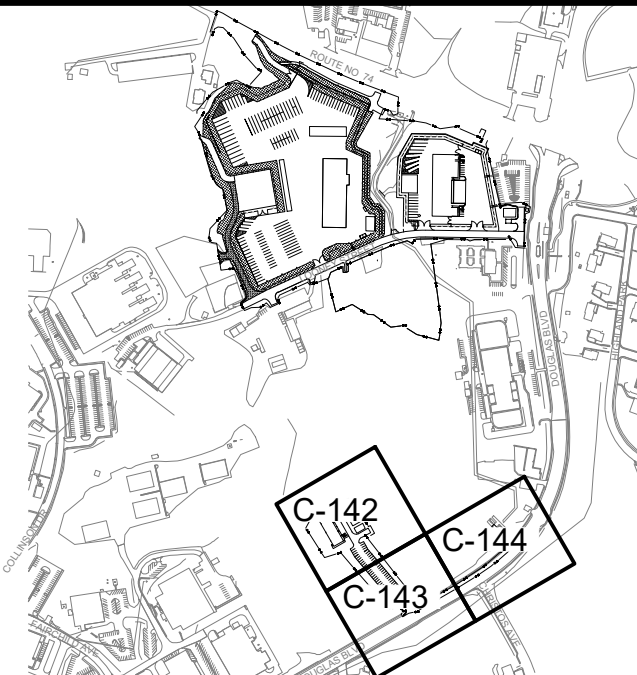

OVERALL EXISTING CONDITION PLAN COF SS (CLIN 0004)


SHEET ID
C-141

INTERMEDIATE DESIGN

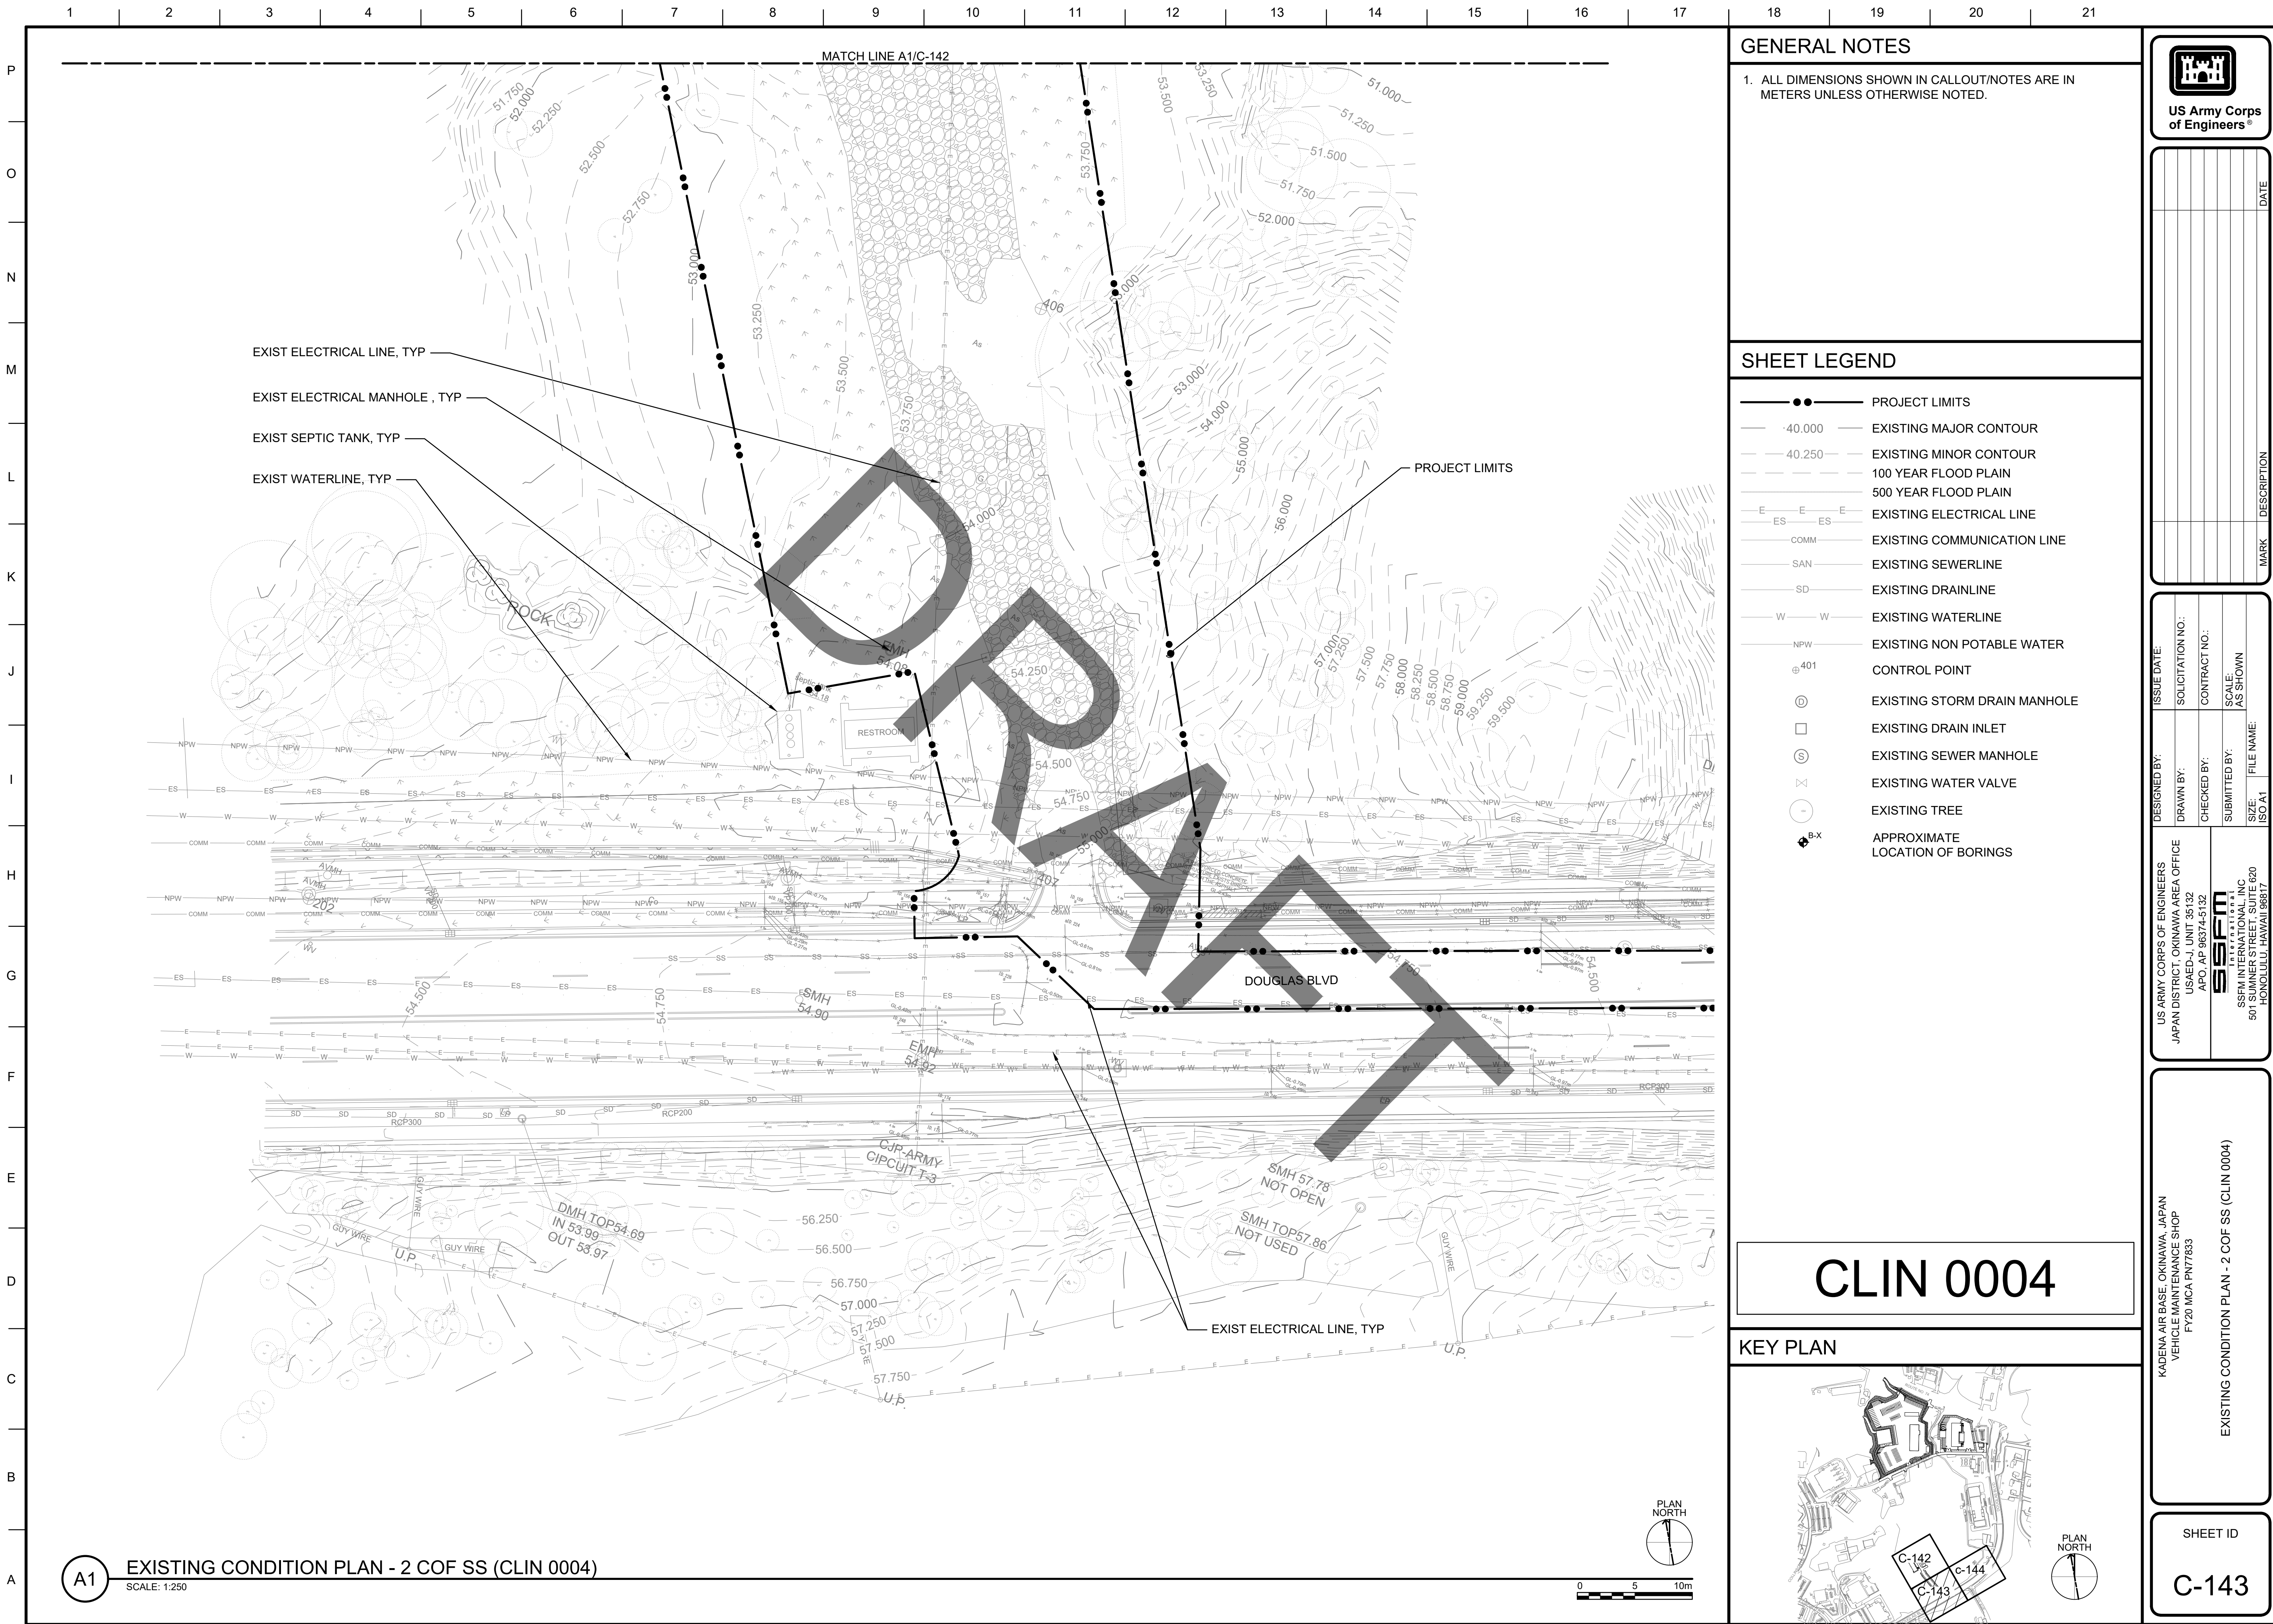



1. ALL DIMENSIONS SHOWN IN CALLOUT/NOTES ARE IN METERS UNLESS OTHERWISE NOTED.

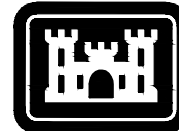

**US Army Corps
of Engineers®**

[illegible]

SHEET LEGEND

	PROJECT LIMITS
	EXISTING MAJOR CONTOUR
	EXISTING MINOR CONTOUR
	100 YEAR FLOOD PLAIN
	500 YEAR FLOOD PLAIN
	EXISTING ELECTRICAL LINE
	EXISTING COMMUNICATION LINE
	EXISTING SEWERLINE
	EXISTING DRAINLINE
	EXISTING WATERLINE
	EXISTING NON POTABLE WATER
	CONTROL POINT
	EXISTING STORM DRAIN MANHOLE
	EXISTING DRAIN INLET
	EXISTING SEWER MANHOLE
	EXISTING WATER VALVE
	EXISTING TREE
	APPROXIMATE LOCATION OF BORINGS


 SSFP INTERNATIONAL 501 SUMNER STREET, SUITE 620 HONOLULU, HAWAII 96817	DESIGNED BY:	ISSUE DATE:
	DRAWN BY:	SOLICITATION NO.:
	CHECKED BY:	CONTRACT NO.:
	SUBMITTED BY:	SCALE:
	SIZE:	AS SHOWN
	ISO A1	FILE NAME:

KADENA AIR BASE OKINAWA JAPAN
VEHICLE MAINTENANCE SHOP
FY20 MCA PN77833

SHEET ID

C-144


KEY PLAN

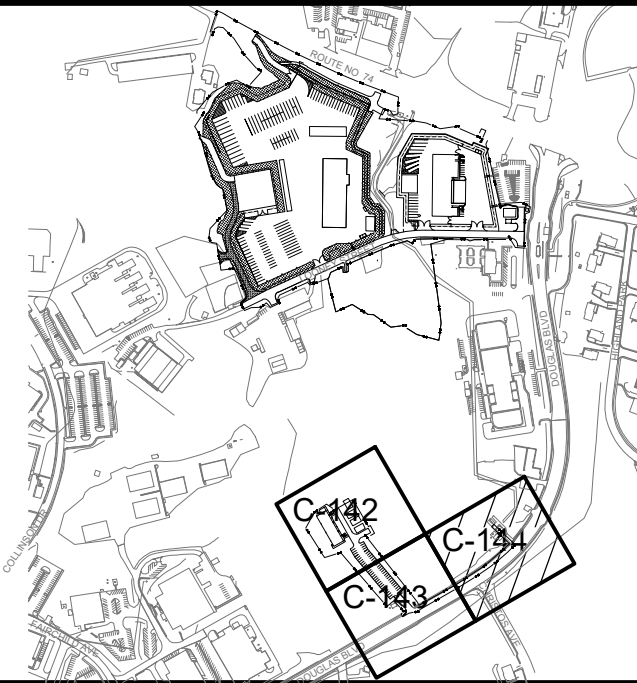

PLAN
NORTH




INTERMEDIATE DESIGN

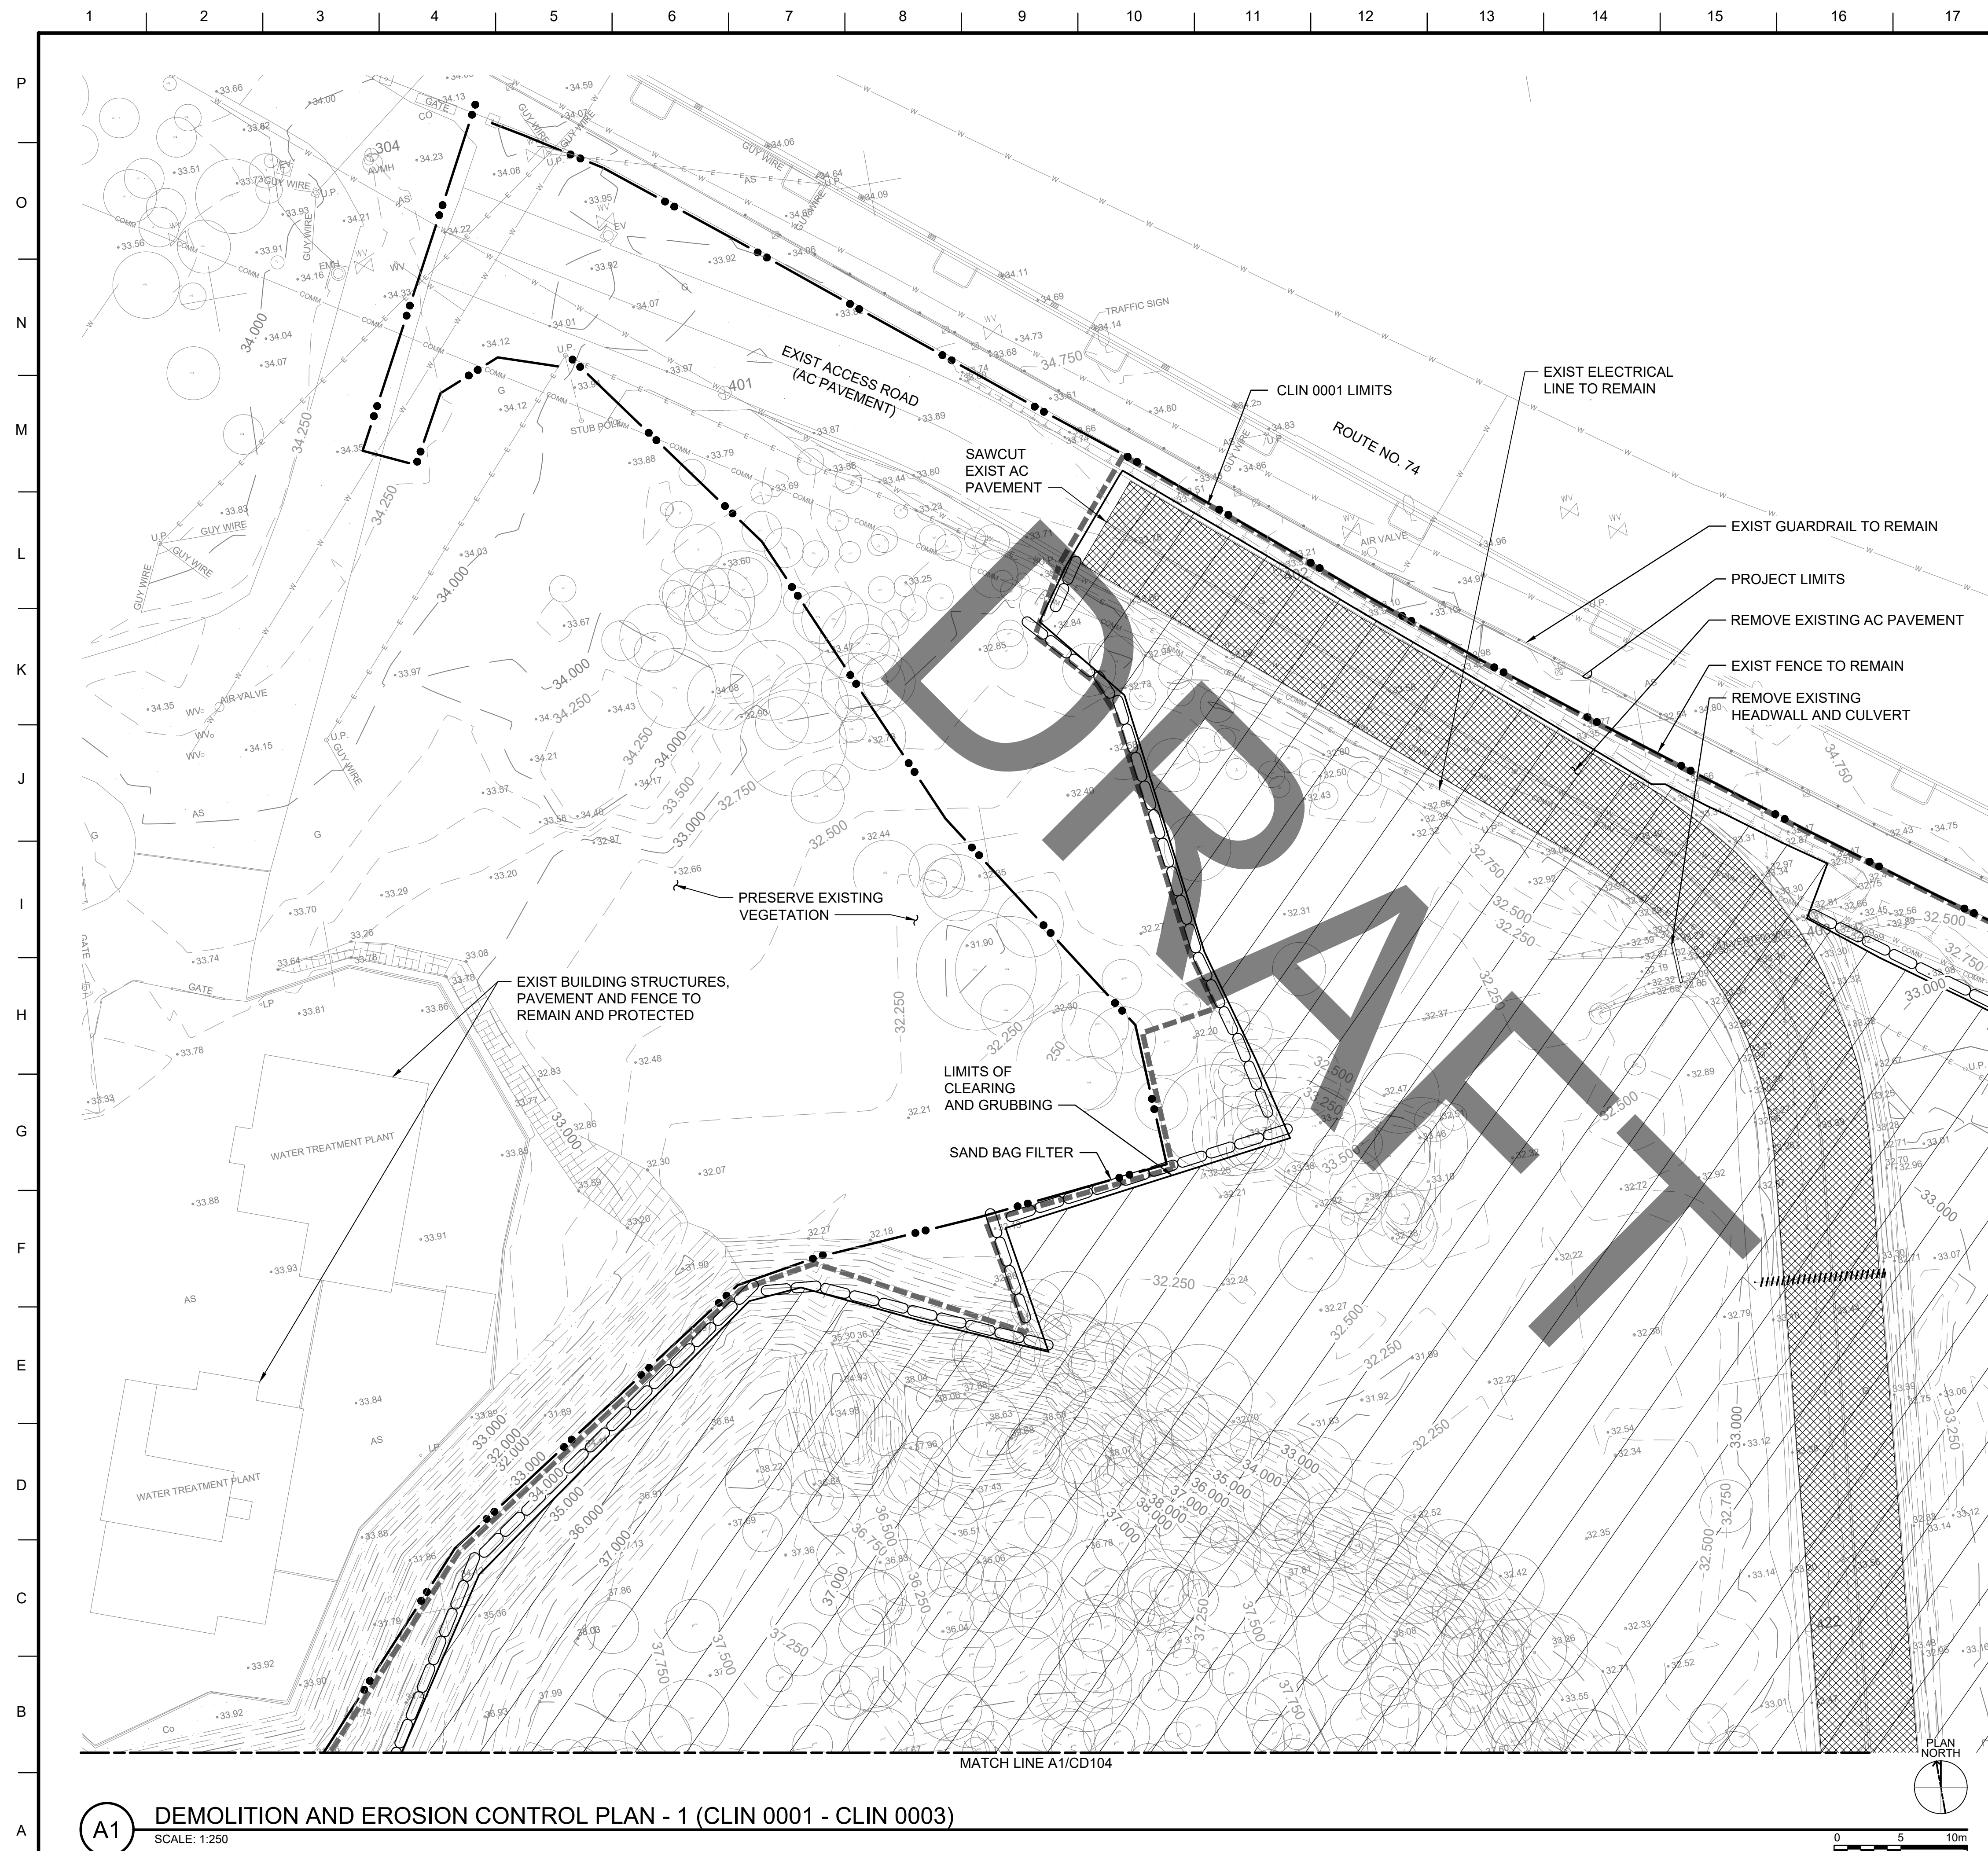



GENERAL NOTES

1. FOR DEMO NOTES, SEE SHEET CD101.
2. FOR LEGENDS AND ABBREVIATIONS, SEE SHEET C-001.

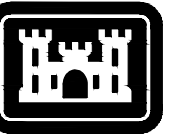


US Army Corps
of Engineers®

SHEET LEGEND

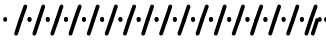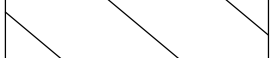- | | |
|---|--|
|  | PROJECT LIMITS |
|  | EXISTING MAJOR CONTOUR |
|  | EXISTING MINOR CONTOUR |
|  | REMOVE EXISTING UTILITIES
AND EXISTING FENCE |
|  | EXISTING ELECTRICAL LINE |
|  | EXISTING SEWERLINE |
|  | EXISTING DRAINLINE |
|  | EXISTING WATERLINE |
|  | DEMOLISH AND REMOVE
EXISTING AC PAVEMENT |
|  | EXISTING BUILDING, CONCRETE BLOCK,
CONTAINER, EXISTING STRUCTURES,
CONCRETE FOUNDATION AND
FOOTINGS REMOVAL |
|  | LIMITS OF CLEARING
AND GRUBBING |

KEY PLAN

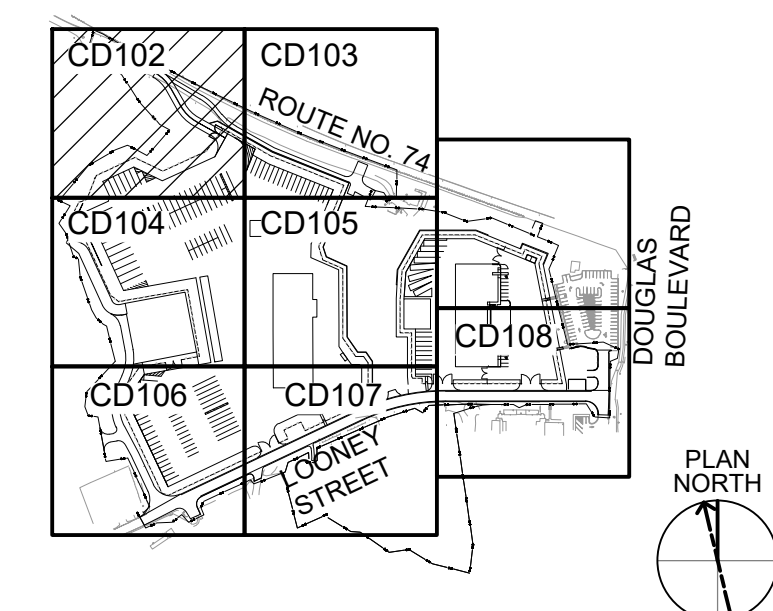

DESIGNED BY:	ISSUE DATE:
US ARMY CORPS OF ENGINEERS	
JAPAN DISTRICT, OKINAWA AREA OFFICE	
AWD-J UNIT 35132	
USED-J UNIT 35132	
	
Ssfm INTERNATIONAL, INC. 501 SUMNER STREET, SUITE 620 HONOLULU, HAWAII 96817	
DRAWN BY:	SOLICITATION NO.:
CHECKED BY:	CONTRACT NO.:
SUBMITTED BY:	SCALE:
	AS SHOWN
SIZE:	FILE NAME:
ISO A1	HONOLULU_HAWAII_96817

KADENA AIR BASE, OKINAWA, JAPAN
VEHICLE MAINTENANCE SHOP
FY20 MCA PN77833

SHEET ID

CD102

INTERMEDIATE DESIGN



GENERAL NOTES




1. FOR DEMO NOTES, SEE SHEET CD101



**U.S. Army Corps
Engineers®**

[illegible]


SHEET LEGEND

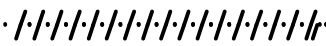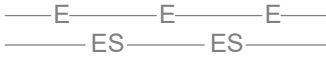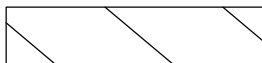	PROJECT LIMITS
	EXISTING MAJOR CONTOUR
	EXISTING MINOR CONTOUR
	REMOVE EXISTING UTILITIES AND EXISTING FENCE
	EXISTING ELECTRICAL LINE
	EXISTING SEWERLINE
	EXISTING DRAINLINE
	EXISTING WATERLINE
	DEMOLISH AND REMOVE EXISTING AC PAVEMENT
	EXISTING BUILDING, CONCRETE BLOCK, CONTAINER, EXISTING STRUCTURES, CONCRETE FOUNDATION AND FOOTINGS REMOVAL
	LIMITS OF CLEARING AND GRUBBING

 SFSM SFSM INTERNATIONAL, INC. 501 SUMNER STREET, SUITE 620 HONOLULU, HAWAII 96817	SHOWN BY:	COLLECTION NO.:
	CHECKED BY:	CONTRACT NO.:
SUBMITTED BY:	SCALE: AS SHOWN	
SIZE:	FILE NAME:	
ISO A1		

CLIN 0001-0003

KEY PLAN

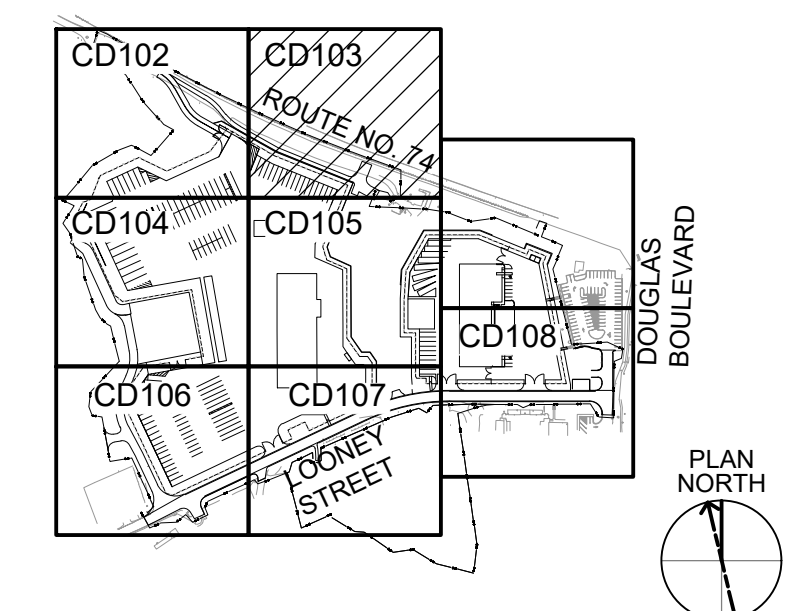


FY20 MCA PN77833

DEMOLITION AND EROSION CONTROL PLAN - 2 (CLIN 0001 - CLIN 0003)

SHEET ID


CD103

INTERMEDIATE DESIGN

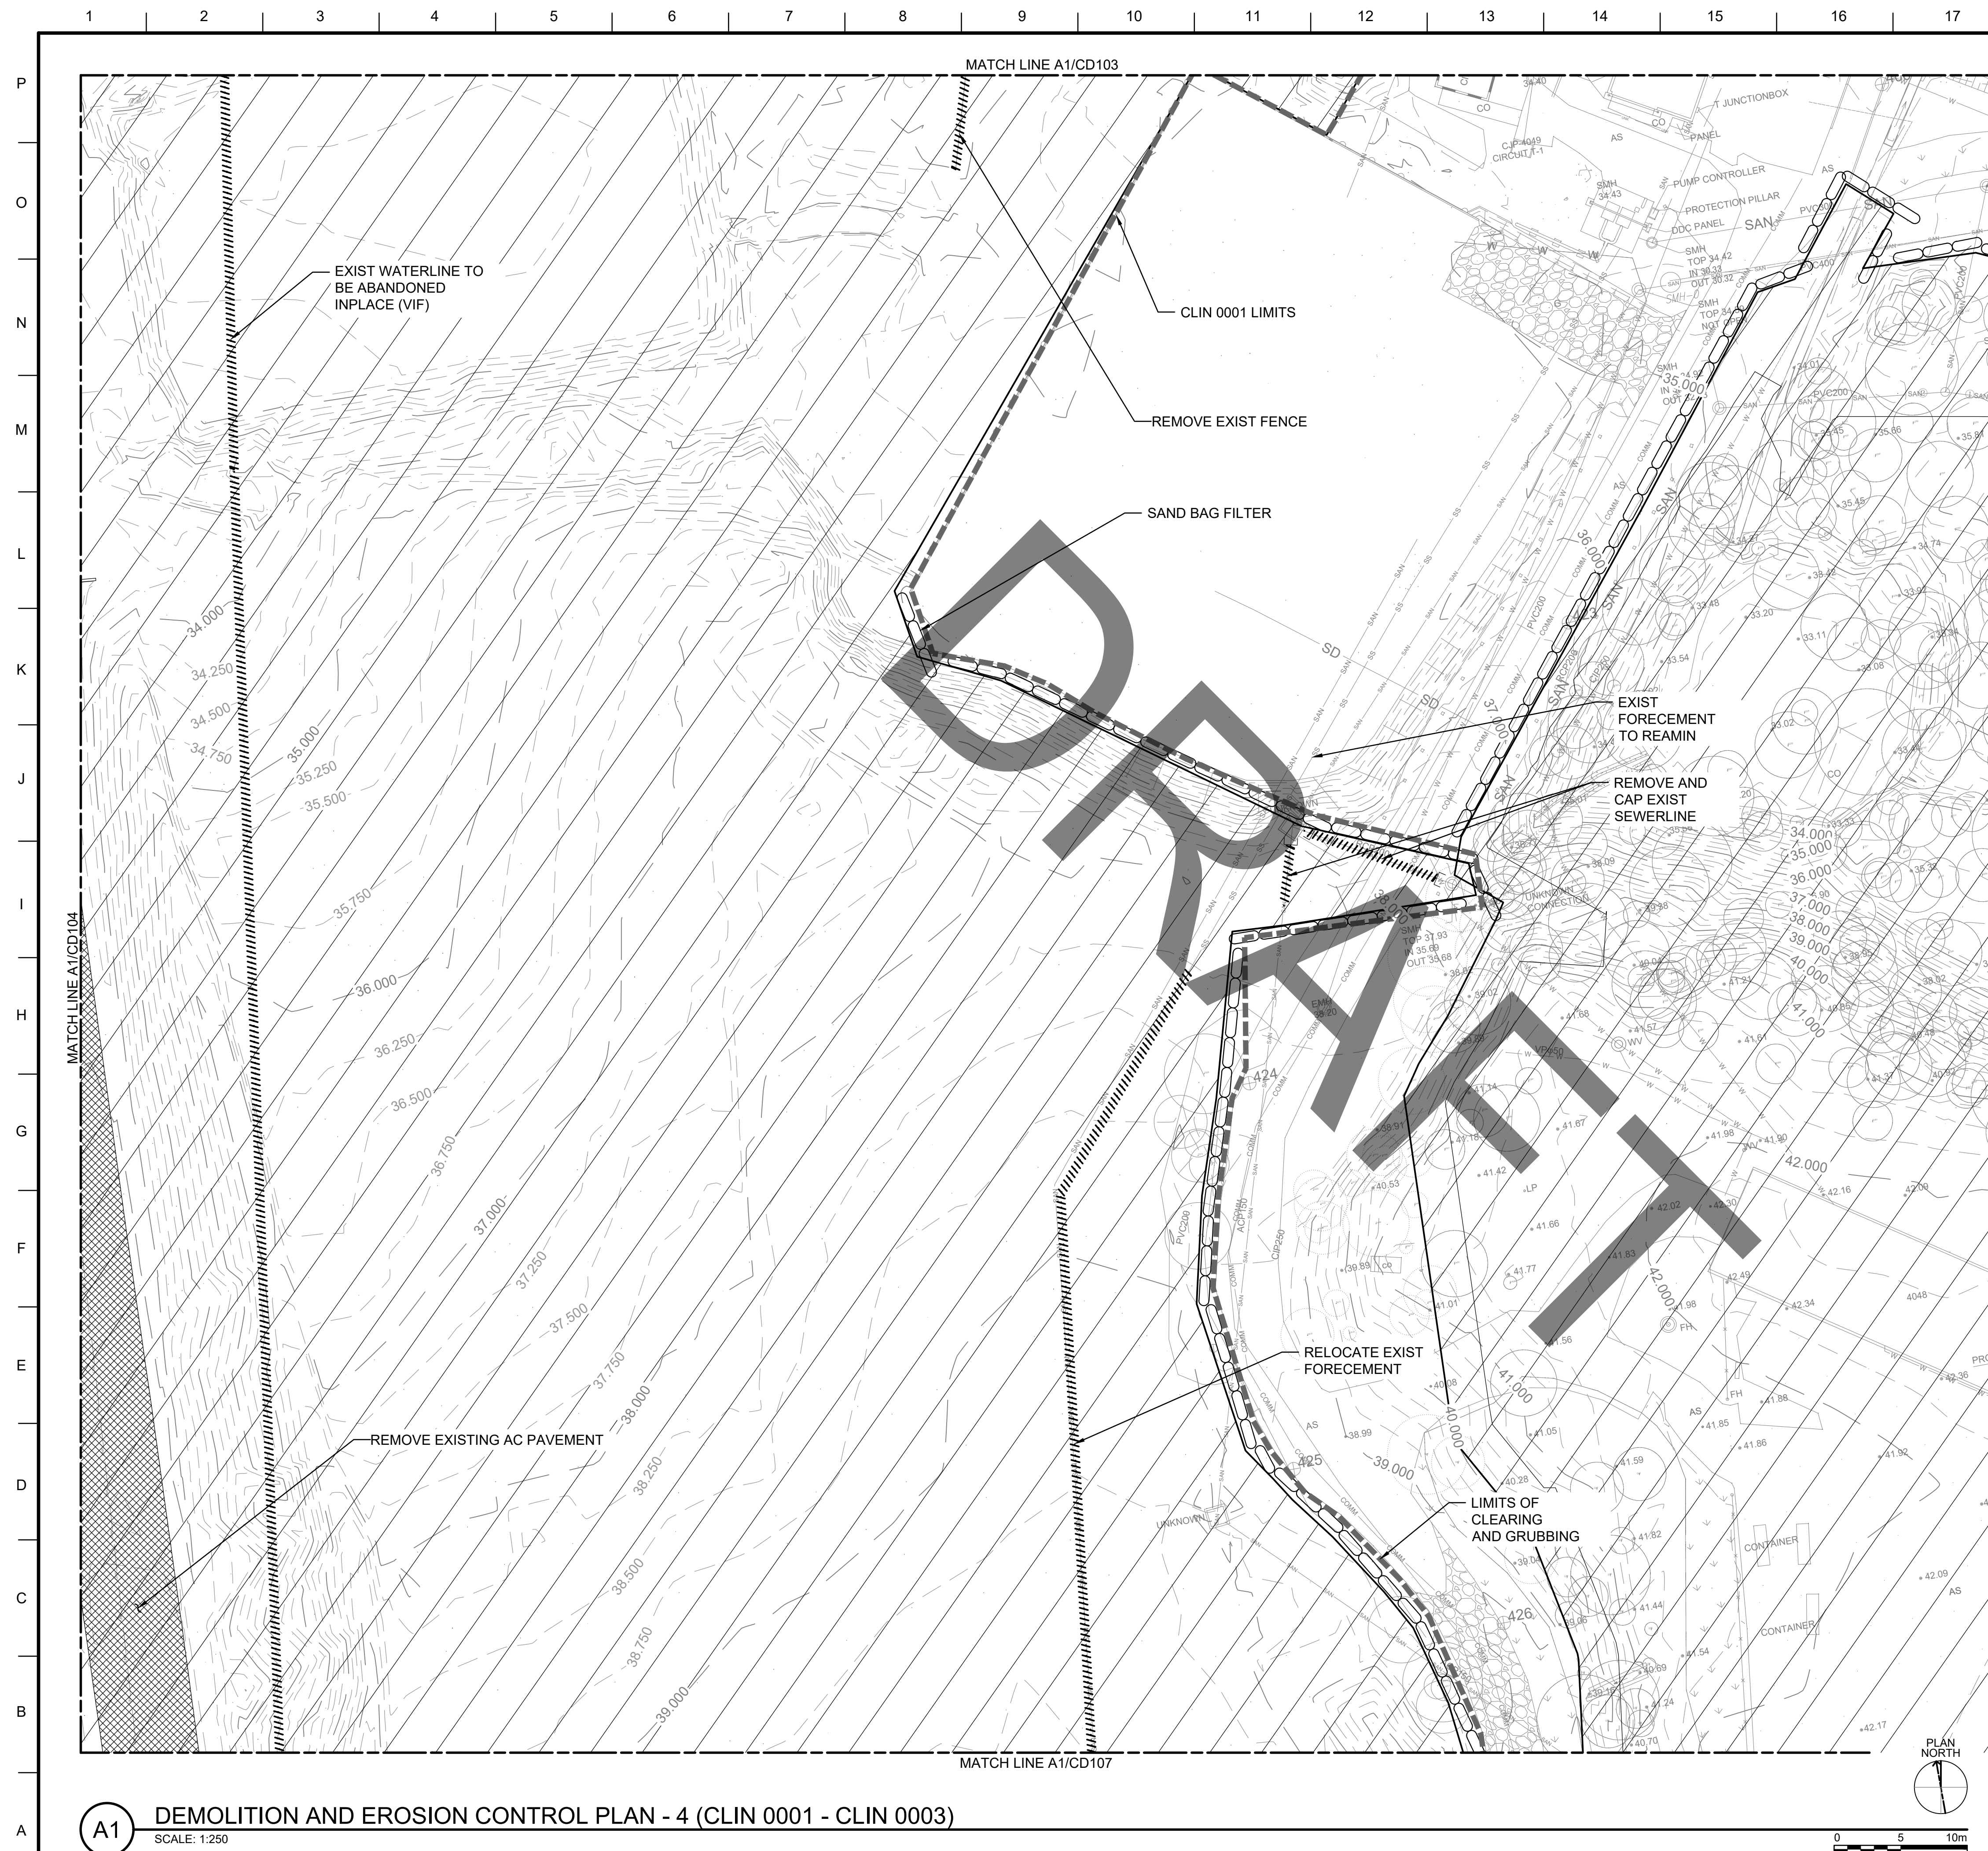


GENERAL NOTES

1. FOR DEMO NOTES, SEE SHEET CD101

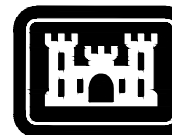


US Army Corps
of Engineers®

SHEET LEGEND

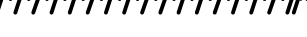- | | |
|---|--|
|  | PROJECT LIMITS |
|  | EXISTING MAJOR CONTOUR |
|  | EXISTING MINOR CONTOUR |
|  | REMOVE EXISTING UTILITIES
AND EXISTING FENCE |
|  | EXISTING ELECTRICAL LINE |
|  | EXISTING SEWERLINE |
|  | EXISTING DRAINLINE |
|  | EXISTING WATERLINE |
|  | DEMOLISH AND REMOVE
EXISTING AC PAVEMENT |
|  | EXISTING BUILDING, CONCRETE BLOCK,
CONTAINER, EXISTING STRUCTURES,
CONCRETE FOUNDATION AND
FOOTINGS REMOVAL |
|  | LIMITS OF CLEARING
AND GRUBBING |

KEY PLAN

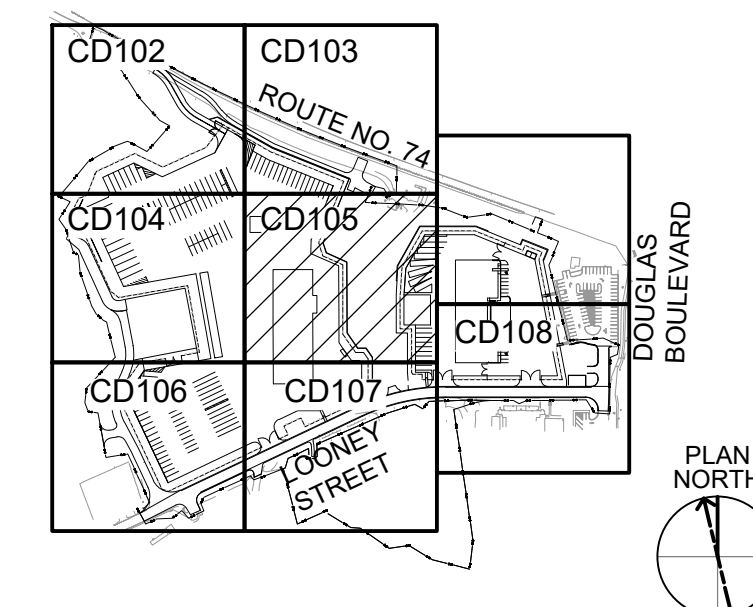


US ARMY CORPS OF ENGINEERS JAPAN DISTRICT, OKINAWA AREA OFFICE USASD-J, UNIT 35132 APO, AP 96374-5132 	DESIGNED BY:	ISSUE DATE:
	DRAWN BY:	SOLICITATION NO.:
	CHECKED BY:	CONTRACT NO.:
	SUBMITTED BY:	SCALE: AS SHOWN
SSFIM INTERNATIONAL, INC 501 SUMNER STREET, SUITE 620 APO, AP 96374-5132		FILE NAME:


KADENA AIR BASE, OKINAWA, JAPAN
VEHICLE MAINTENANCE SHOP
FY20 MCA PN77833

SHEET ID


CD105

INTERMEDIATE DESIGN

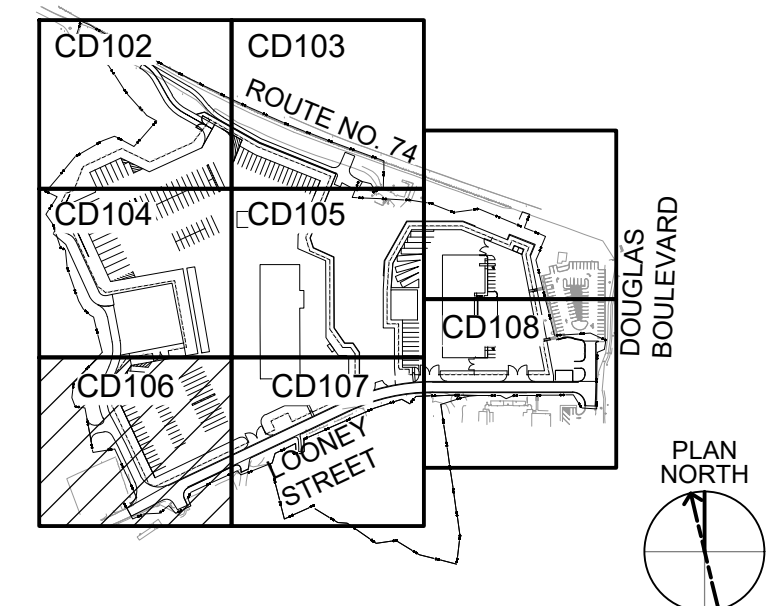

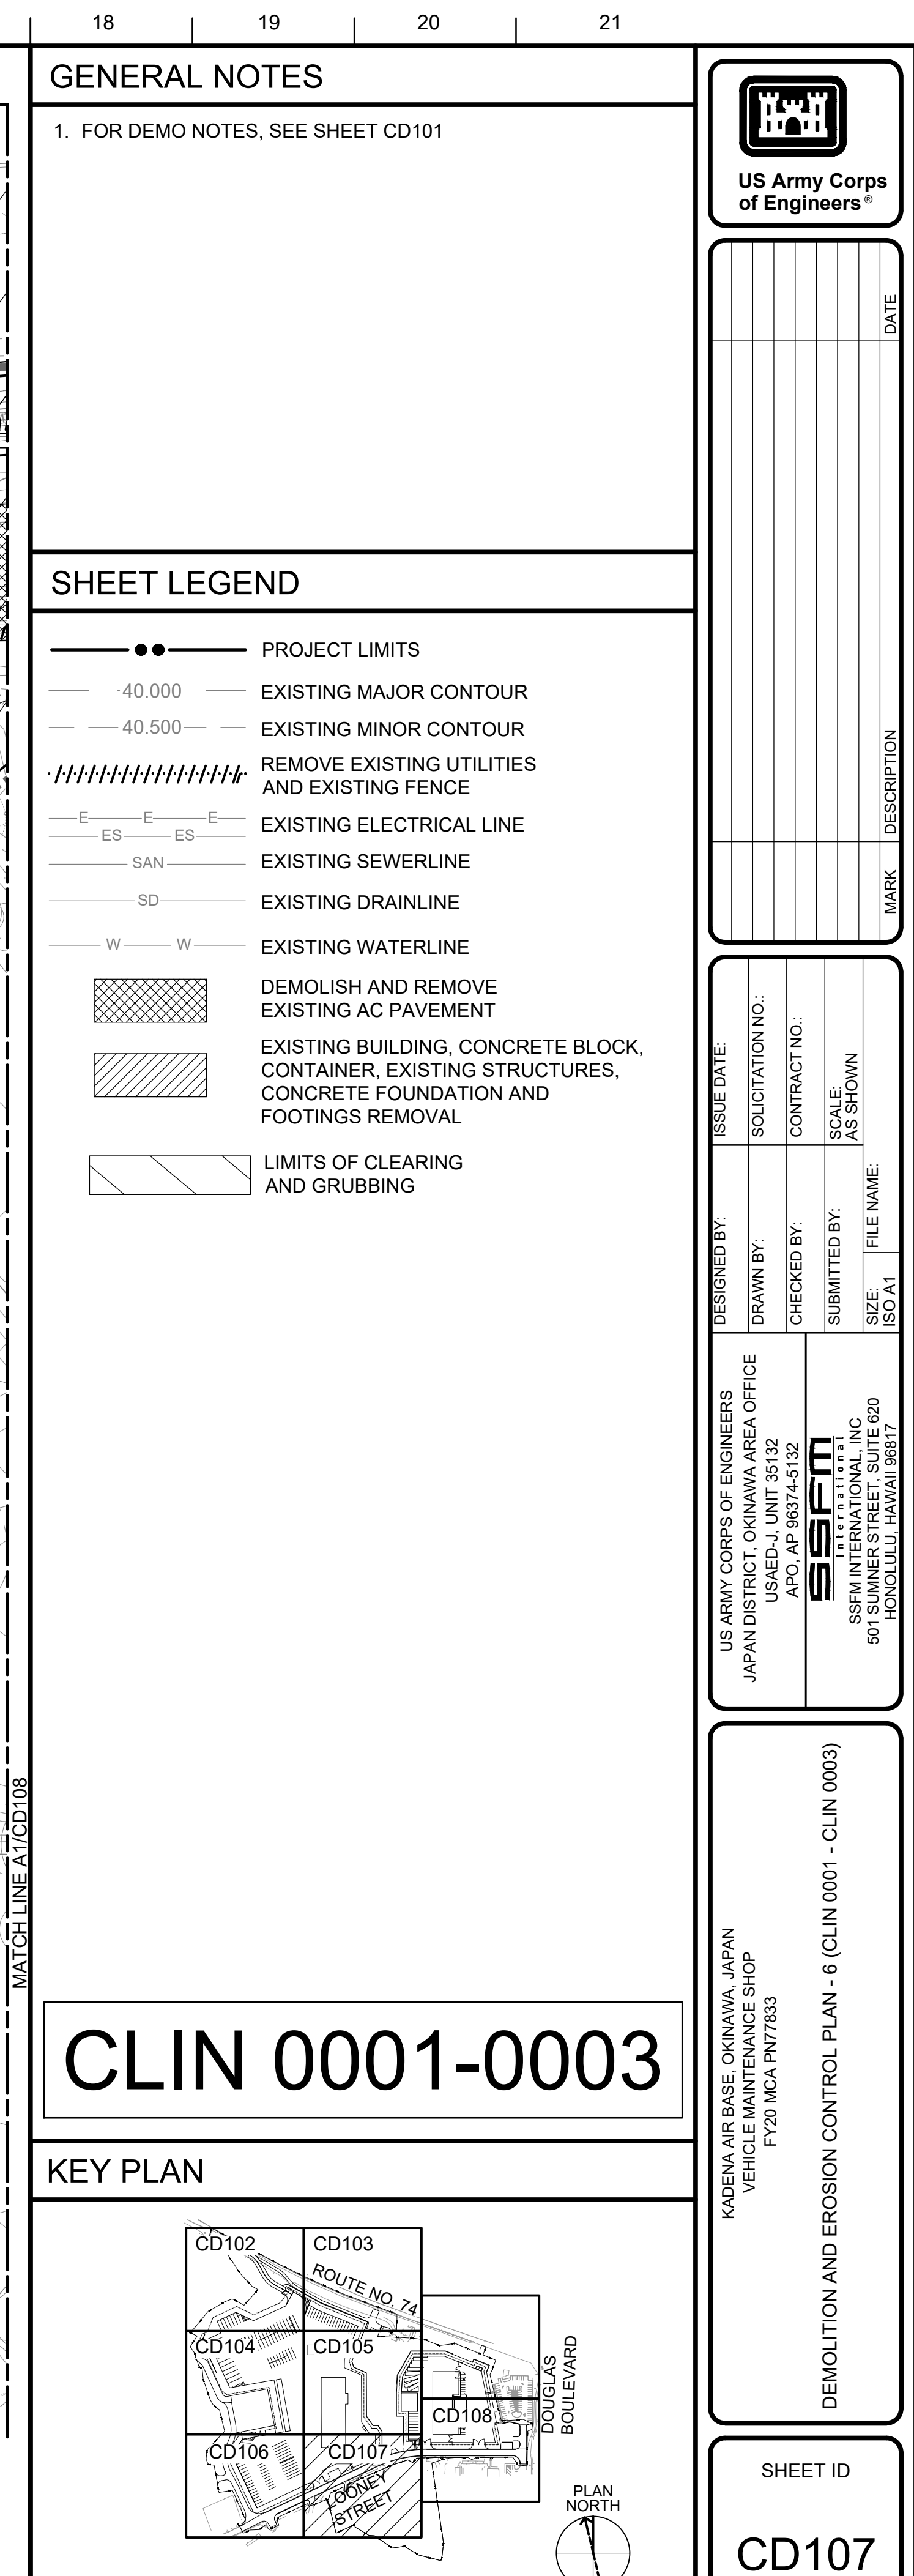

INTERMEDIATE DESIGN

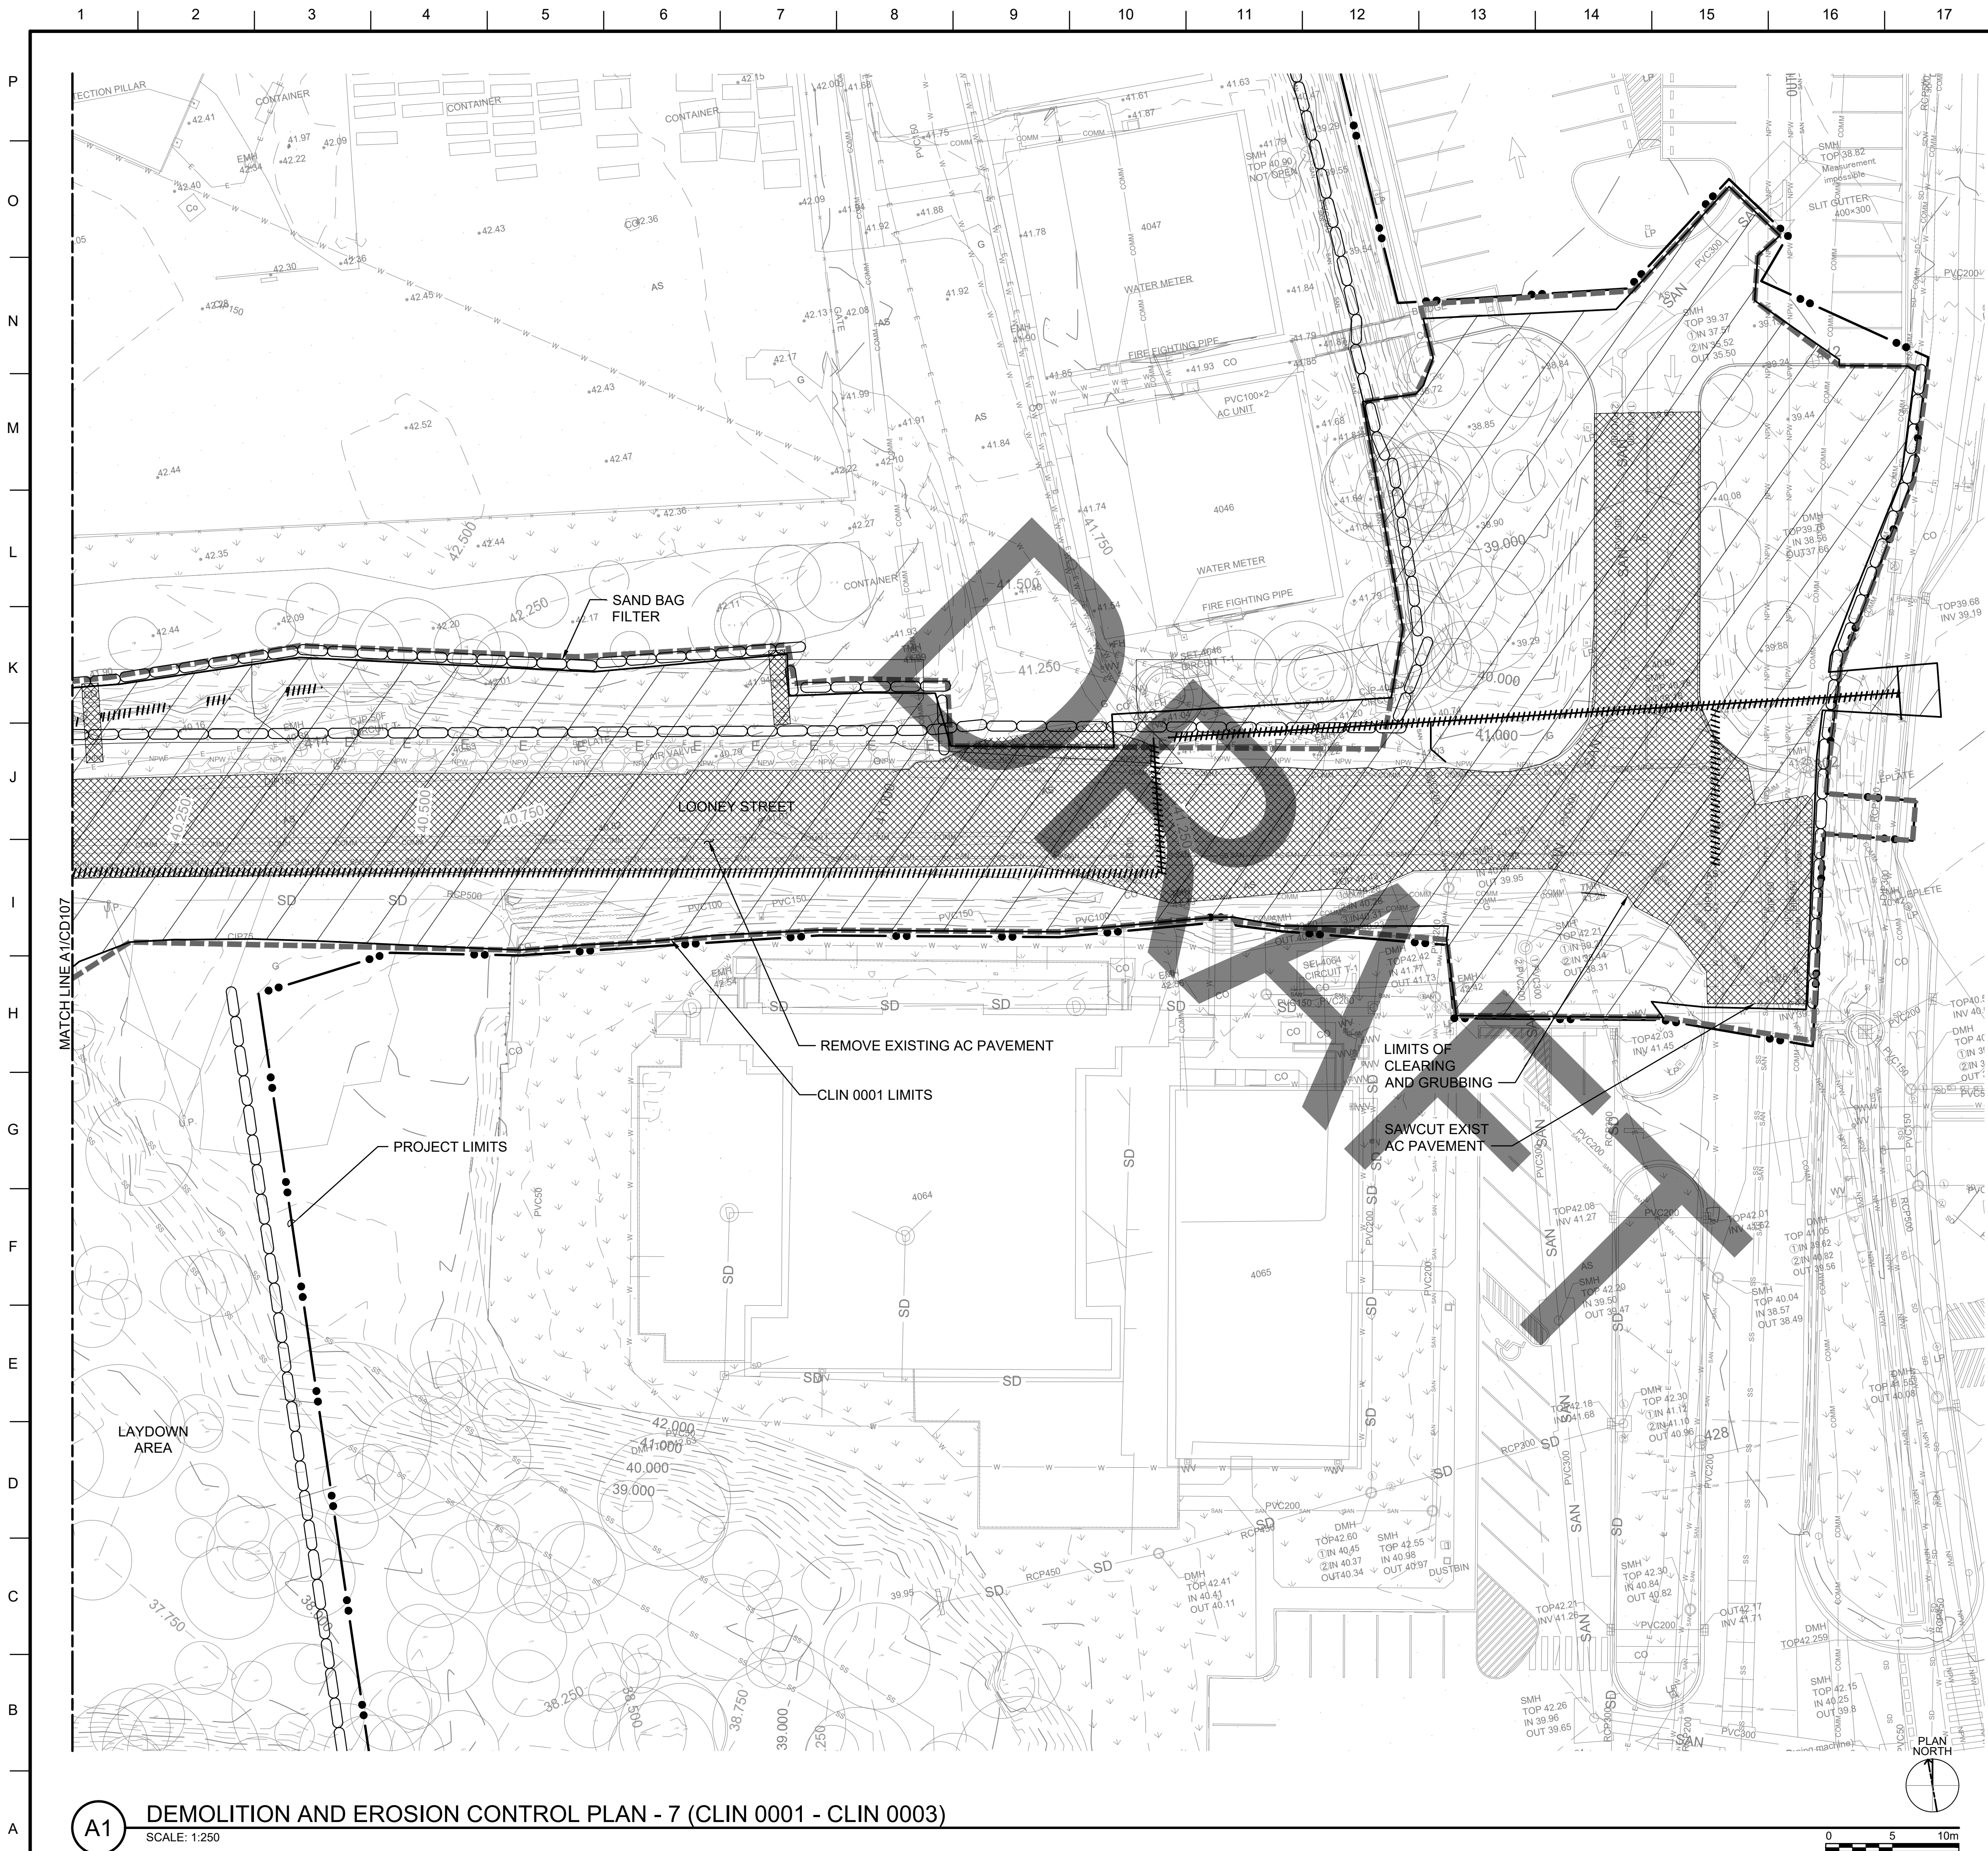

A1 DEMOLITION AND EROSION CONTROL PLAN - 7 (CLIN 0001 - CLIN 0003)
SCALE: 1:250

GENERAL NOTES


1. FOR DEMO NOTES, SEE SHEET CD101

SHEET LEGEND

- PROJECT LIMITS
- EXISTING MAJOR CONTOUR
- EXISTING MINOR CONTOUR
- REMOVE EXISTING UTILITIES AND EXISTING FENCE
- EXISTING ELECTRICAL LINE
- EXISTING SEWERLINE
- EXISTING DRAINLINE
- EXISTING WATERLINE
- DEMOLISH AND REMOVE EXISTING AC PAVEMENT
- EXISTING BUILDING, CONCRETE BLOCK, CONTAINER, EXISTING STRUCTURES, CONCRETE FOUNDATION AND FOOTINGS REMOVAL
- LIMITS OF CLEARING AND GRUBBING

CLIN 0001-0003

KEY PLAN

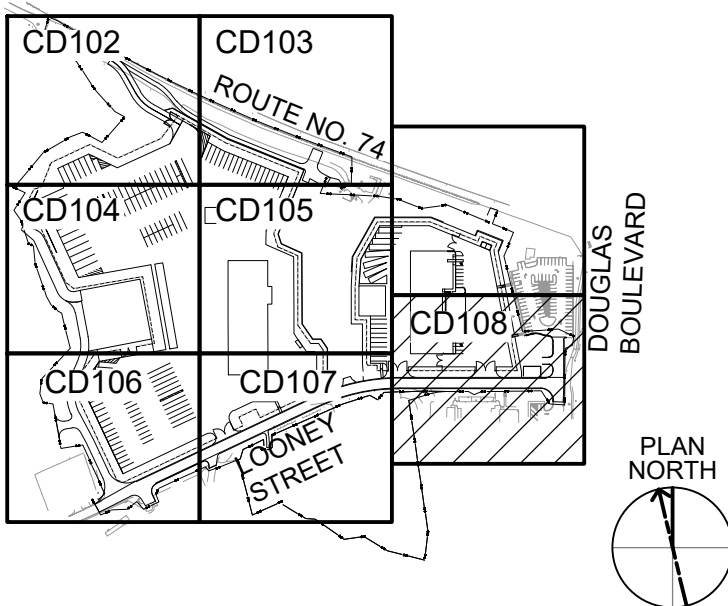

US Army Corps of Engineers

ISSUE DATE:		SOLICITATION NO.:		CONTRACT NO.:	
DESIGNED BY:	DRAWN BY:	CHECKED BY:	SUBMITTED BY:	SCALE:	AS SHOWN
US ARMY CORPS OF ENGINEERS JAPAN DISTRICT, OKINAWA AREA OFFICE USAFD-J UNIT 35132 APO, AP 96374-5132		SSEM INTERNATIONAL, INC. 501 SUMNER STREET, SUITE 620 HONOLULU, HAWAII 96817		FILE NAME:	ISO A1


KADENA AIR BASE, OKINAWA, JAPAN
VEHICLE MAINTENANCE SHOP
FY20 MCA PN77833

DEMOLITION AND EROSION CONTROL PLAN - 7 (CLIN 0001 - CLIN 0003)

SHEET ID

CD108

INTERMEDIATE DESIGN

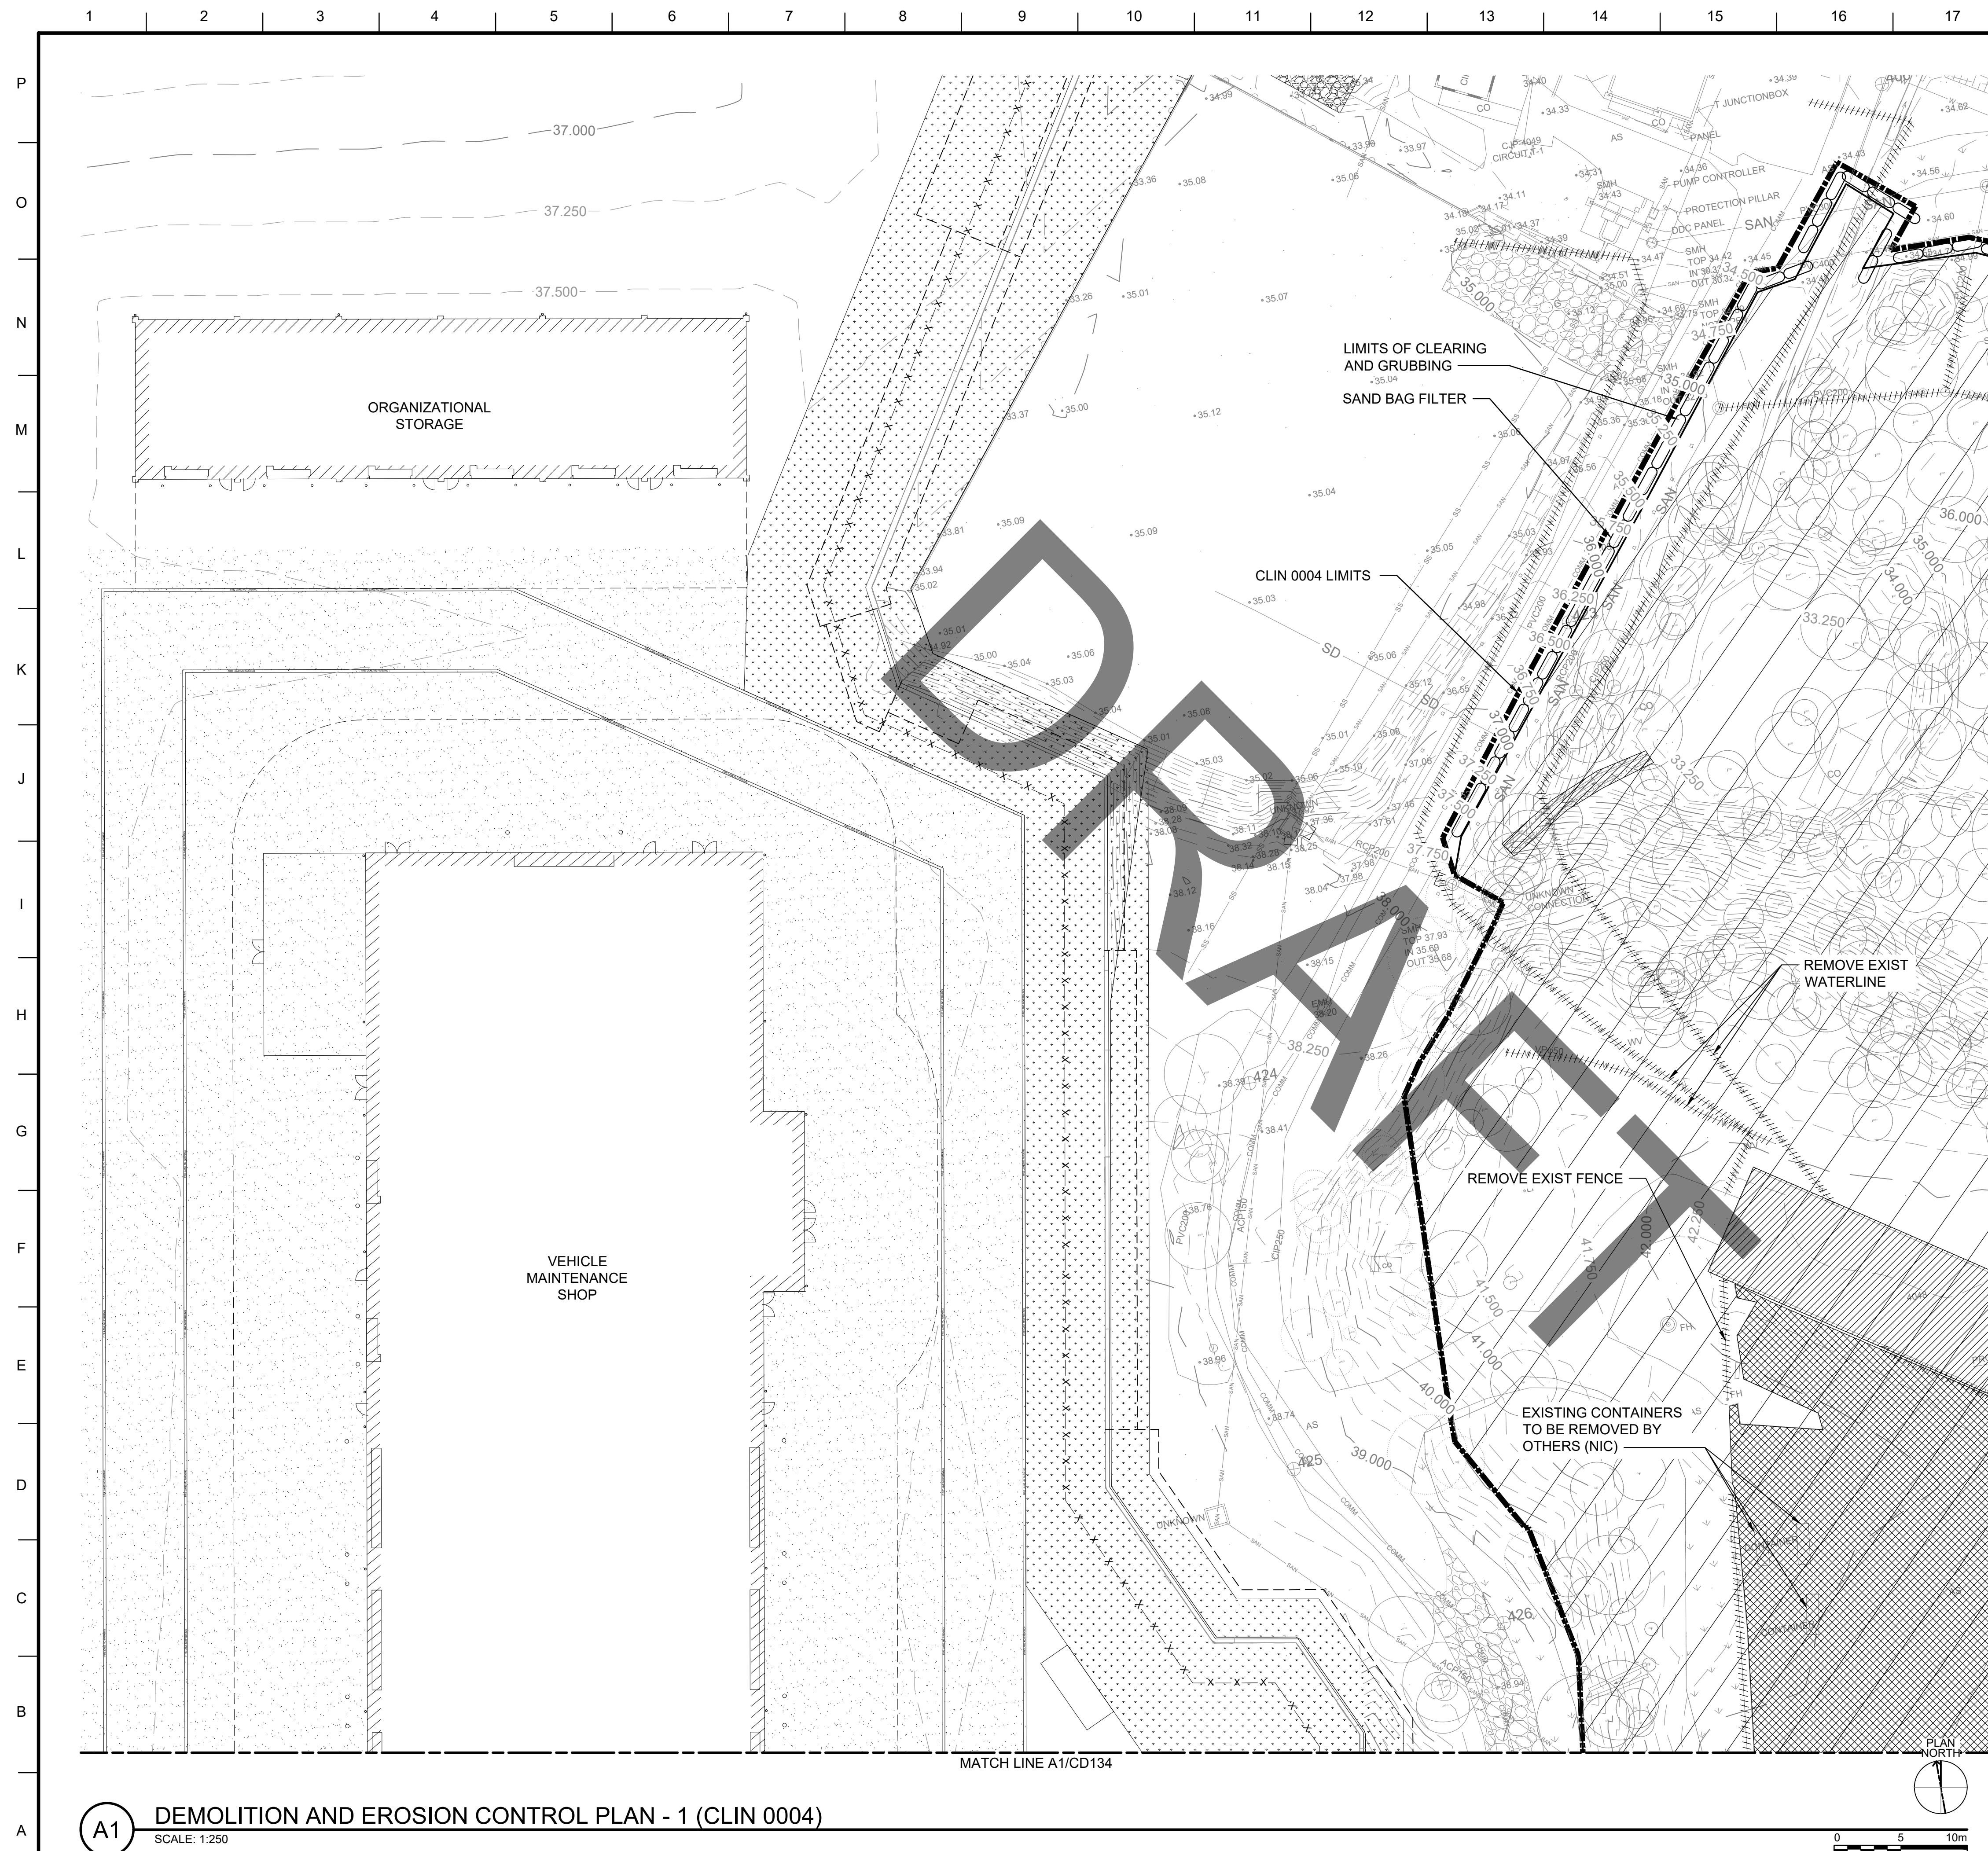



GENERAL NOTES

1. FOR DEMO NOTES, SEE SHEET CD101




**U.S. Army Corps
Engineers®**

SHEET LEGEND

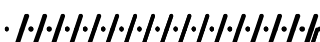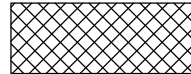- | | |
|---|---|
|  | PROJECT LIMITS |
|  | EXISTING MAJOR CONTOUR |
|  | EXISTING MINOR CONTOUR |
|  | REMOVE EXISTING UTILITIES
AND EXISTING FENCE |
|  | EXISTING ELECTRICAL LINE |
|  | EXISTING SEWERLINE |
|  | EXISTING DRAINLINE |
|  | EXISTING WATERLINE |
|  | DEMOLISH AND REMOVE
EXISTING AC PAVEMENT |
|  | EXISTING BUILDING, CONCRETE BLOCK,
CONTAINER, EXISTING STRUCTURES,
CONCRETE FOUNDATION AND
FOOTINGS REMOVAL |
|  | CLIN 0004:
TEMPORARY FACILITIES (COF SS)
DEMOLITION OF 8 EXISTING BUILDINGS
SITE PREPARATION, FENCING, AND
CLEARING OF SSA
SUPPLY SUPPORT ACTIVITY (SSA)
WAREHOUSE STORAGE SHED FOR SSA
PARKING AND PAVING FOR SSA |


KEY PLAN

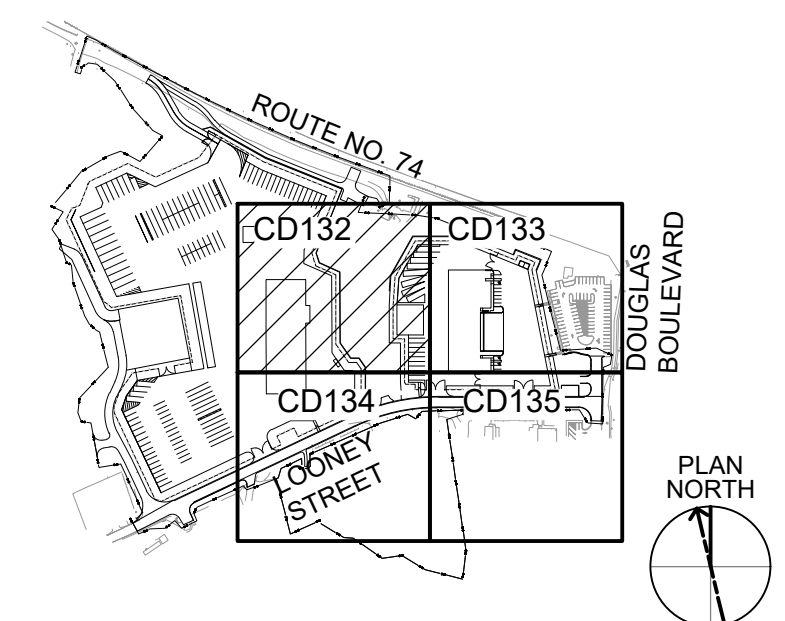

NAJENKIN BASE, OKINAWA, JAPAN
VEHICLE MAINTENANCE SHOP
FY20 MCA PN77833


SHEET ID
CD132

INTERMEDIATE DESIGN

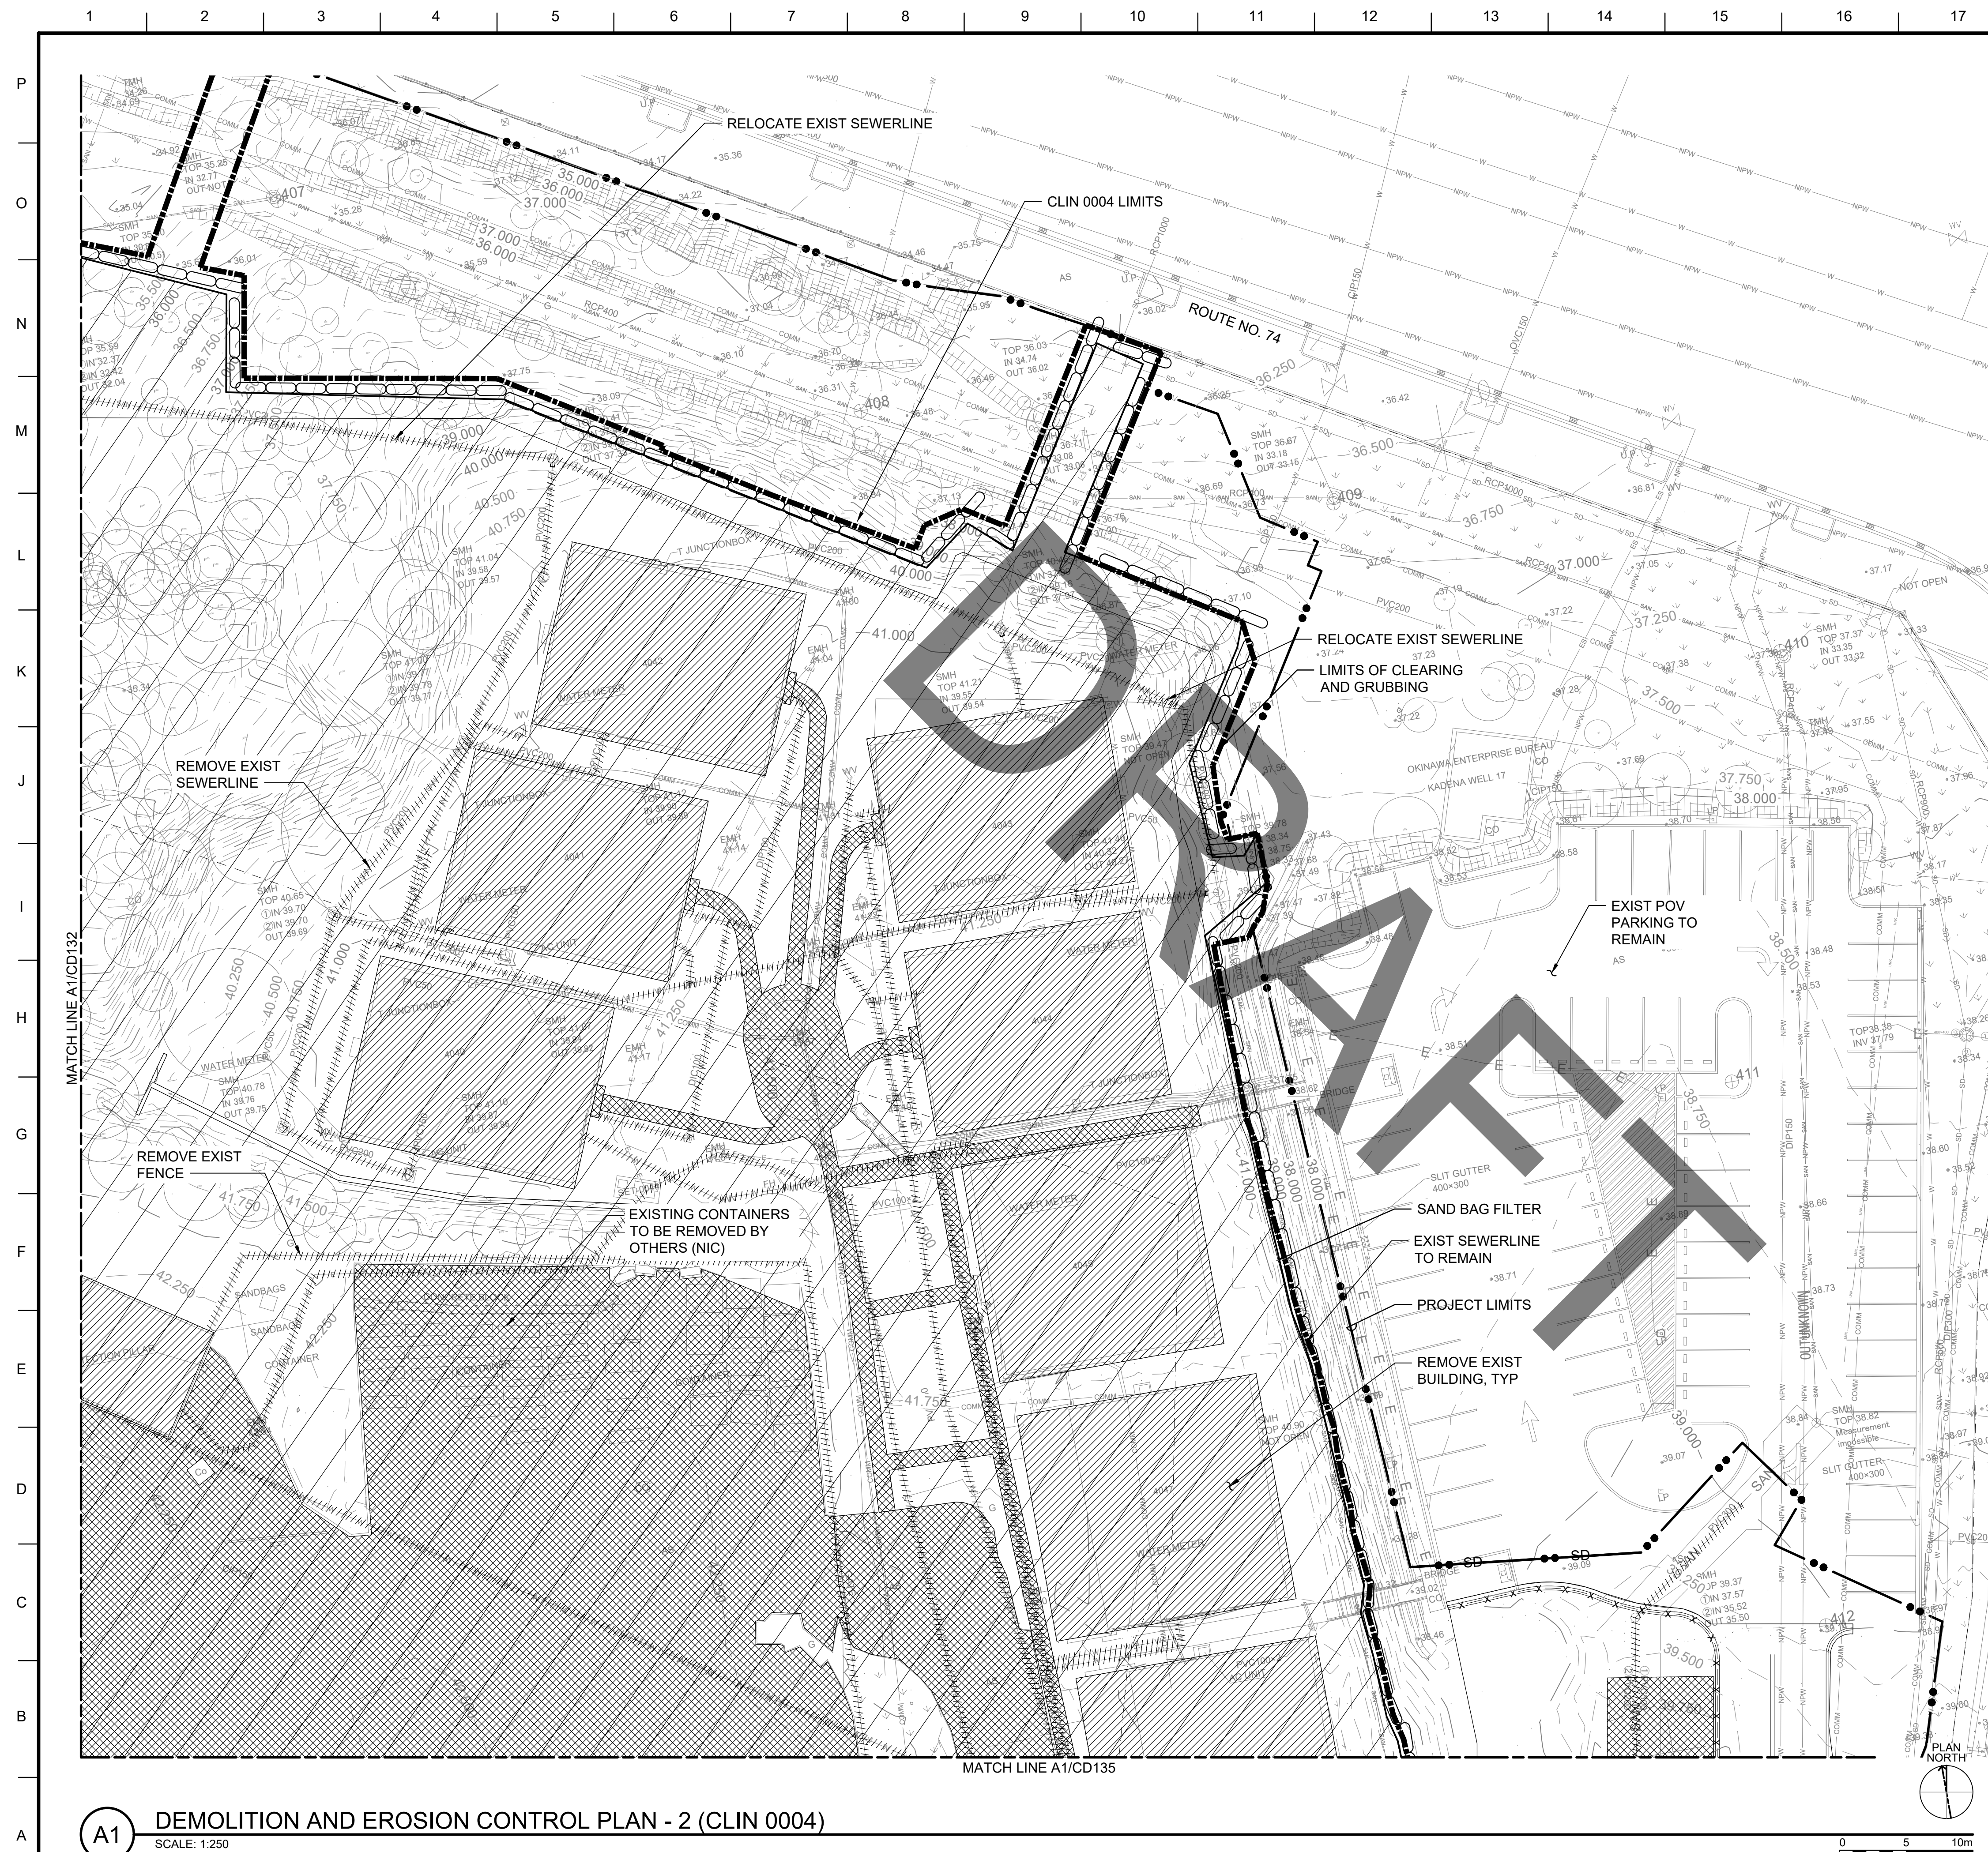






GENERAL NOTES

1. FOR DEMO NOTES, SEE SHEET CD101

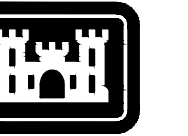


**U.S. Army Corps
Engineers®**

SHEET LEGEND

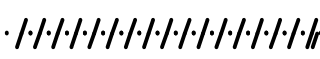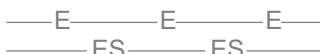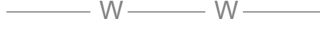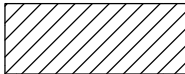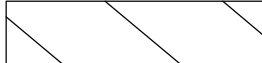- | | |
|---|---|
|  | PROJECT LIMITS |
|  | EXISTING MAJOR CONTOUR |
|  | EXISTING MINOR CONTOUR |
|  | REMOVE EXISTING UTILITIES
AND EXISTING FENCE |
|  | EXISTING ELECTRICAL LINE |
|  | EXISTING SEWERLINE |
|  | EXISTING DRAINLINE |
|  | EXISTING WATERLINE |
|  | DEMOLISH AND REMOVE
EXISTING AC PAVEMENT |
|  | EXISTING BUILDING, CONCRETE BLOCK,
CONTAINER, EXISTING STRUCTURES,
CONCRETE FOUNDATION AND
FOOTINGS REMOVAL |
|  | CLIN 0004:
TEMPORARY FACILITIES (COF SS)
DEMOLITION OF 8 EXISTING BUILDINGS
SITE PREPARATION, FENCING, AND
CLEARING OF SSA
SUPPLY SUPPORT ACTIVITY (SSA)
WAREHOUSE STORAGE SHED FOR SSA
PARKING AND PAVING FOR SSA |
|  | LIMITS OF CLEARING
AND GRUBBING |

KEY PLAN

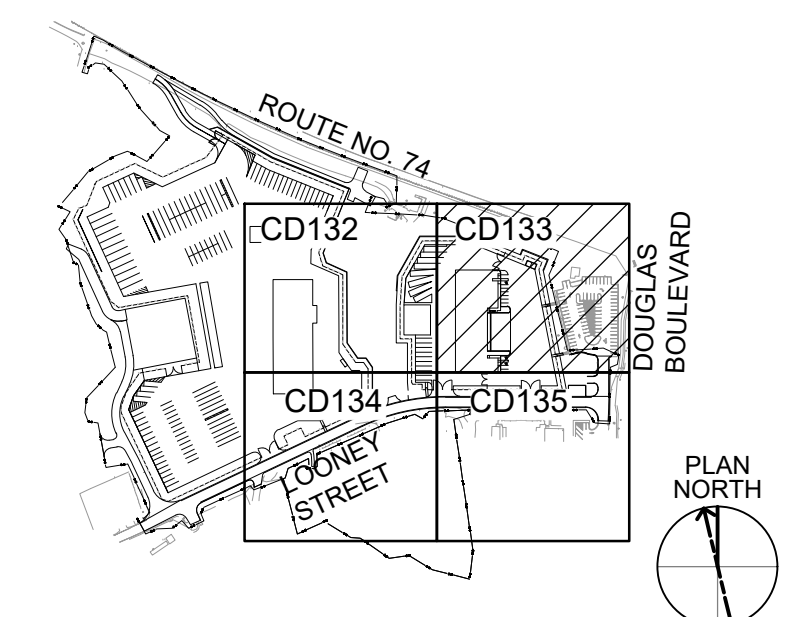[illegible]

JAPAN DISTRICT, OKINAWA AREA OFFICE USAED-J Unit 36132 APO, AP 96374-5132	DRAWN BY:		SOLICITATION NO.:
	CHECKED BY:	CONTRACT NO.:	
 SSM INTERNATIONAL, INC. 501 SUMNER STREET, SUITE 620 HONOLULU, HAWAII 96817	SUBMITTED BY:		SCALE: AS SHOWN
	SIZE: ISO A1	FILE NAME:	

DEMOLITION AND EROSION CONTROL PLAN - 2 (CLIN 0004)
NADEGAR BASE, OKINAWA, JAPAN
VEHICLE MAINTENANCE SHOP
FY20 MCA PN177833


SHEET ID
CD133

INTERMEDIATE DESIGN




GENERAL NOTES

1. FOR DEMO NOTES, SEE SHEET CD101

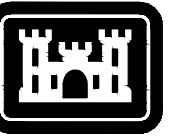


US Army Corps
of Engineers®

SHEET LEGEND

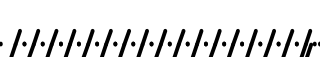- | | |
|---|---|
|  | PROJECT LIMITS |
|  | EXISTING MAJOR CONTOUR |
|  | EXISTING MINOR CONTOUR |
|  | REMOVE EXISTING UTILITIES
AND EXISTING FENCE |
|  | EXISTING ELECTRICAL LINE |
|  | EXISTING SEWERLINE |
|  | EXISTING DRAINLINE |
|  | EXISTING WATERLINE |
|  | DEMOLISH AND REMOVE
EXISTING AC PAVEMENT |
|  | EXISTING BUILDING, CONCRETE BLOCK,
CONTAINER, EXISTING STRUCTURES,
CONCRETE FOUNDATION AND
FOOTINGS REMOVAL |
|  | CLIN 0004:
TEMPORARY FACILITIES (COF SS)
DEMOLITION OF 8 EXISTING BUILDINGS
SITE PREPARATION, FENCING, AND
CLEARING OF SSA
SUPPLY SUPPORT ACTIVITY (SSA)
WAREHOUSE STORAGE SHED FOR SSA
PARKING AND PAVING FOR SSA |

KEY PLAN

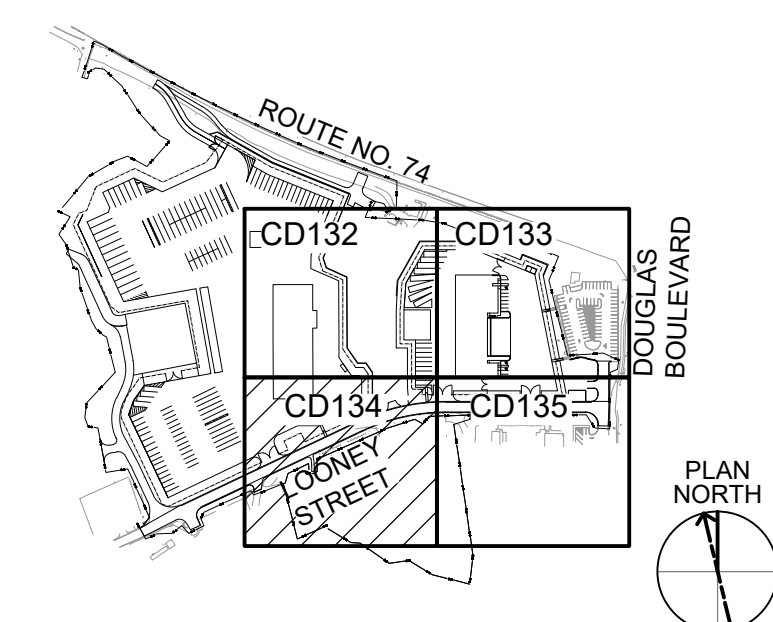

N DISTRICT, OKINAWA AREA OFFICE		DRAWN BY:		SOLICITATION NO.:	
USAFS-1 UNIT 35132		CHECKED BY:		CONTRACT NO.:	
APO AP 96374-5132		SUBMITTED BY:		SCALE:	
 SSFM INTERNATIONAL, INC. 307 SUMNER STREET, SUITE 620 HONOLULU, HAWAII 96817		FILE NAME:		AS SHOWN	
		SIZE:		ISO A1	

NAJENAKIR BASE, OKINAWA, JAPAN
VEHICLE MAINTENANCE SHOP
FY20 MCA PN77833

SHEET ID

CD134

INTERMEDIATE DESIGN



A1 DEMOLITION AND EROSION CONTROL PLAN - 4 (CLIN 0004)
SCALE: 1:250

GENERAL NOTES


1. FOR DEMO NOTES, SEE SHEET CD101

SHEET LEGEND

- PROJECT LIMITS
- EXISTING MAJOR CONTOUR
- EXISTING MINOR CONTOUR
- REMOVE EXISTING UTILITIES AND EXISTING FENCE
- EXISTING ELECTRICAL LINE
- EXISTING SEWERLINE
- EXISTING DRAINLINE
- EXISTING WATERLINE
- DEMOLISH AND REMOVE EXISTING AC PAVEMENT
- EXISTING BUILDING, CONCRETE BLOCK, CONTAINER, EXISTING STRUCTURES, CONCRETE FOUNDATION AND FOOTINGS REMOVAL
- CLIN 0004:
TEMPORARY FACILITIES (COF SS)
DEMOLITION OF 8 EXISTING BUILDINGS
SITE PREPARATION, FENCING, AND CLEARING OF SSA
SUPPLY SUPPORT ACTIVITY (SSA)
WAREHOUSE STORAGE SHED FOR SSA
PARKING AND PAVING FOR SSA

CLIN 0004

KEY PLAN

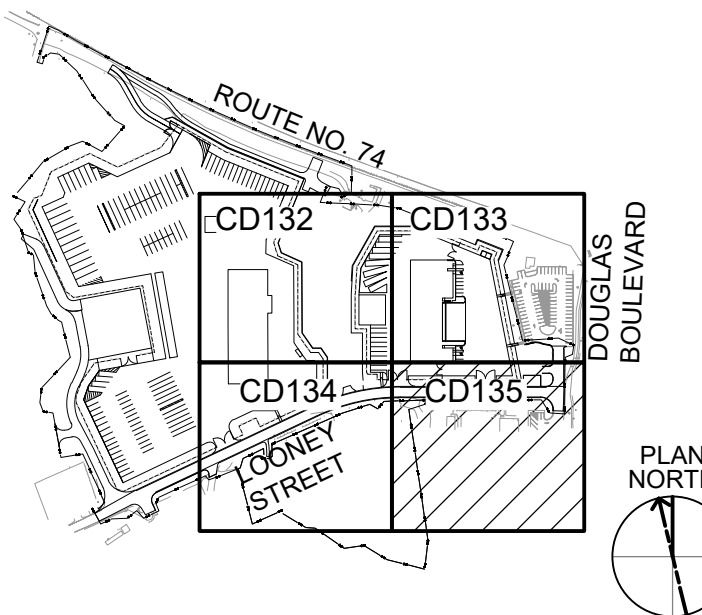

US Army Corps of Engineers®


ISSUE DATE:		SOLICITATION NO.:		CONTRACT NO.:	
DESIGNED BY:		DRAWN BY:		CHECKED BY:	
US ARMY CORPS OF ENGINEERS		JAPAN DISTRICT, OKINAWA AREA OFFICE		APO, AP 96374-5132	
ISSUED-J. UNIT 35132		APO, AP 96374-5132		SSM INTERNATIONAL, INC.	
501 SUMNER STREET, SUITE 620		HONOLULU, HAWAII 96817		SCALE: AS SHOWN	
SIZE: ISO A1		FILE NAME:		MARK	


DEMOLITION AND EROSION CONTROL PLAN - 4 (CLIN 0004)

SHEET ID

CD135

INTERMEDIATE DESIGN

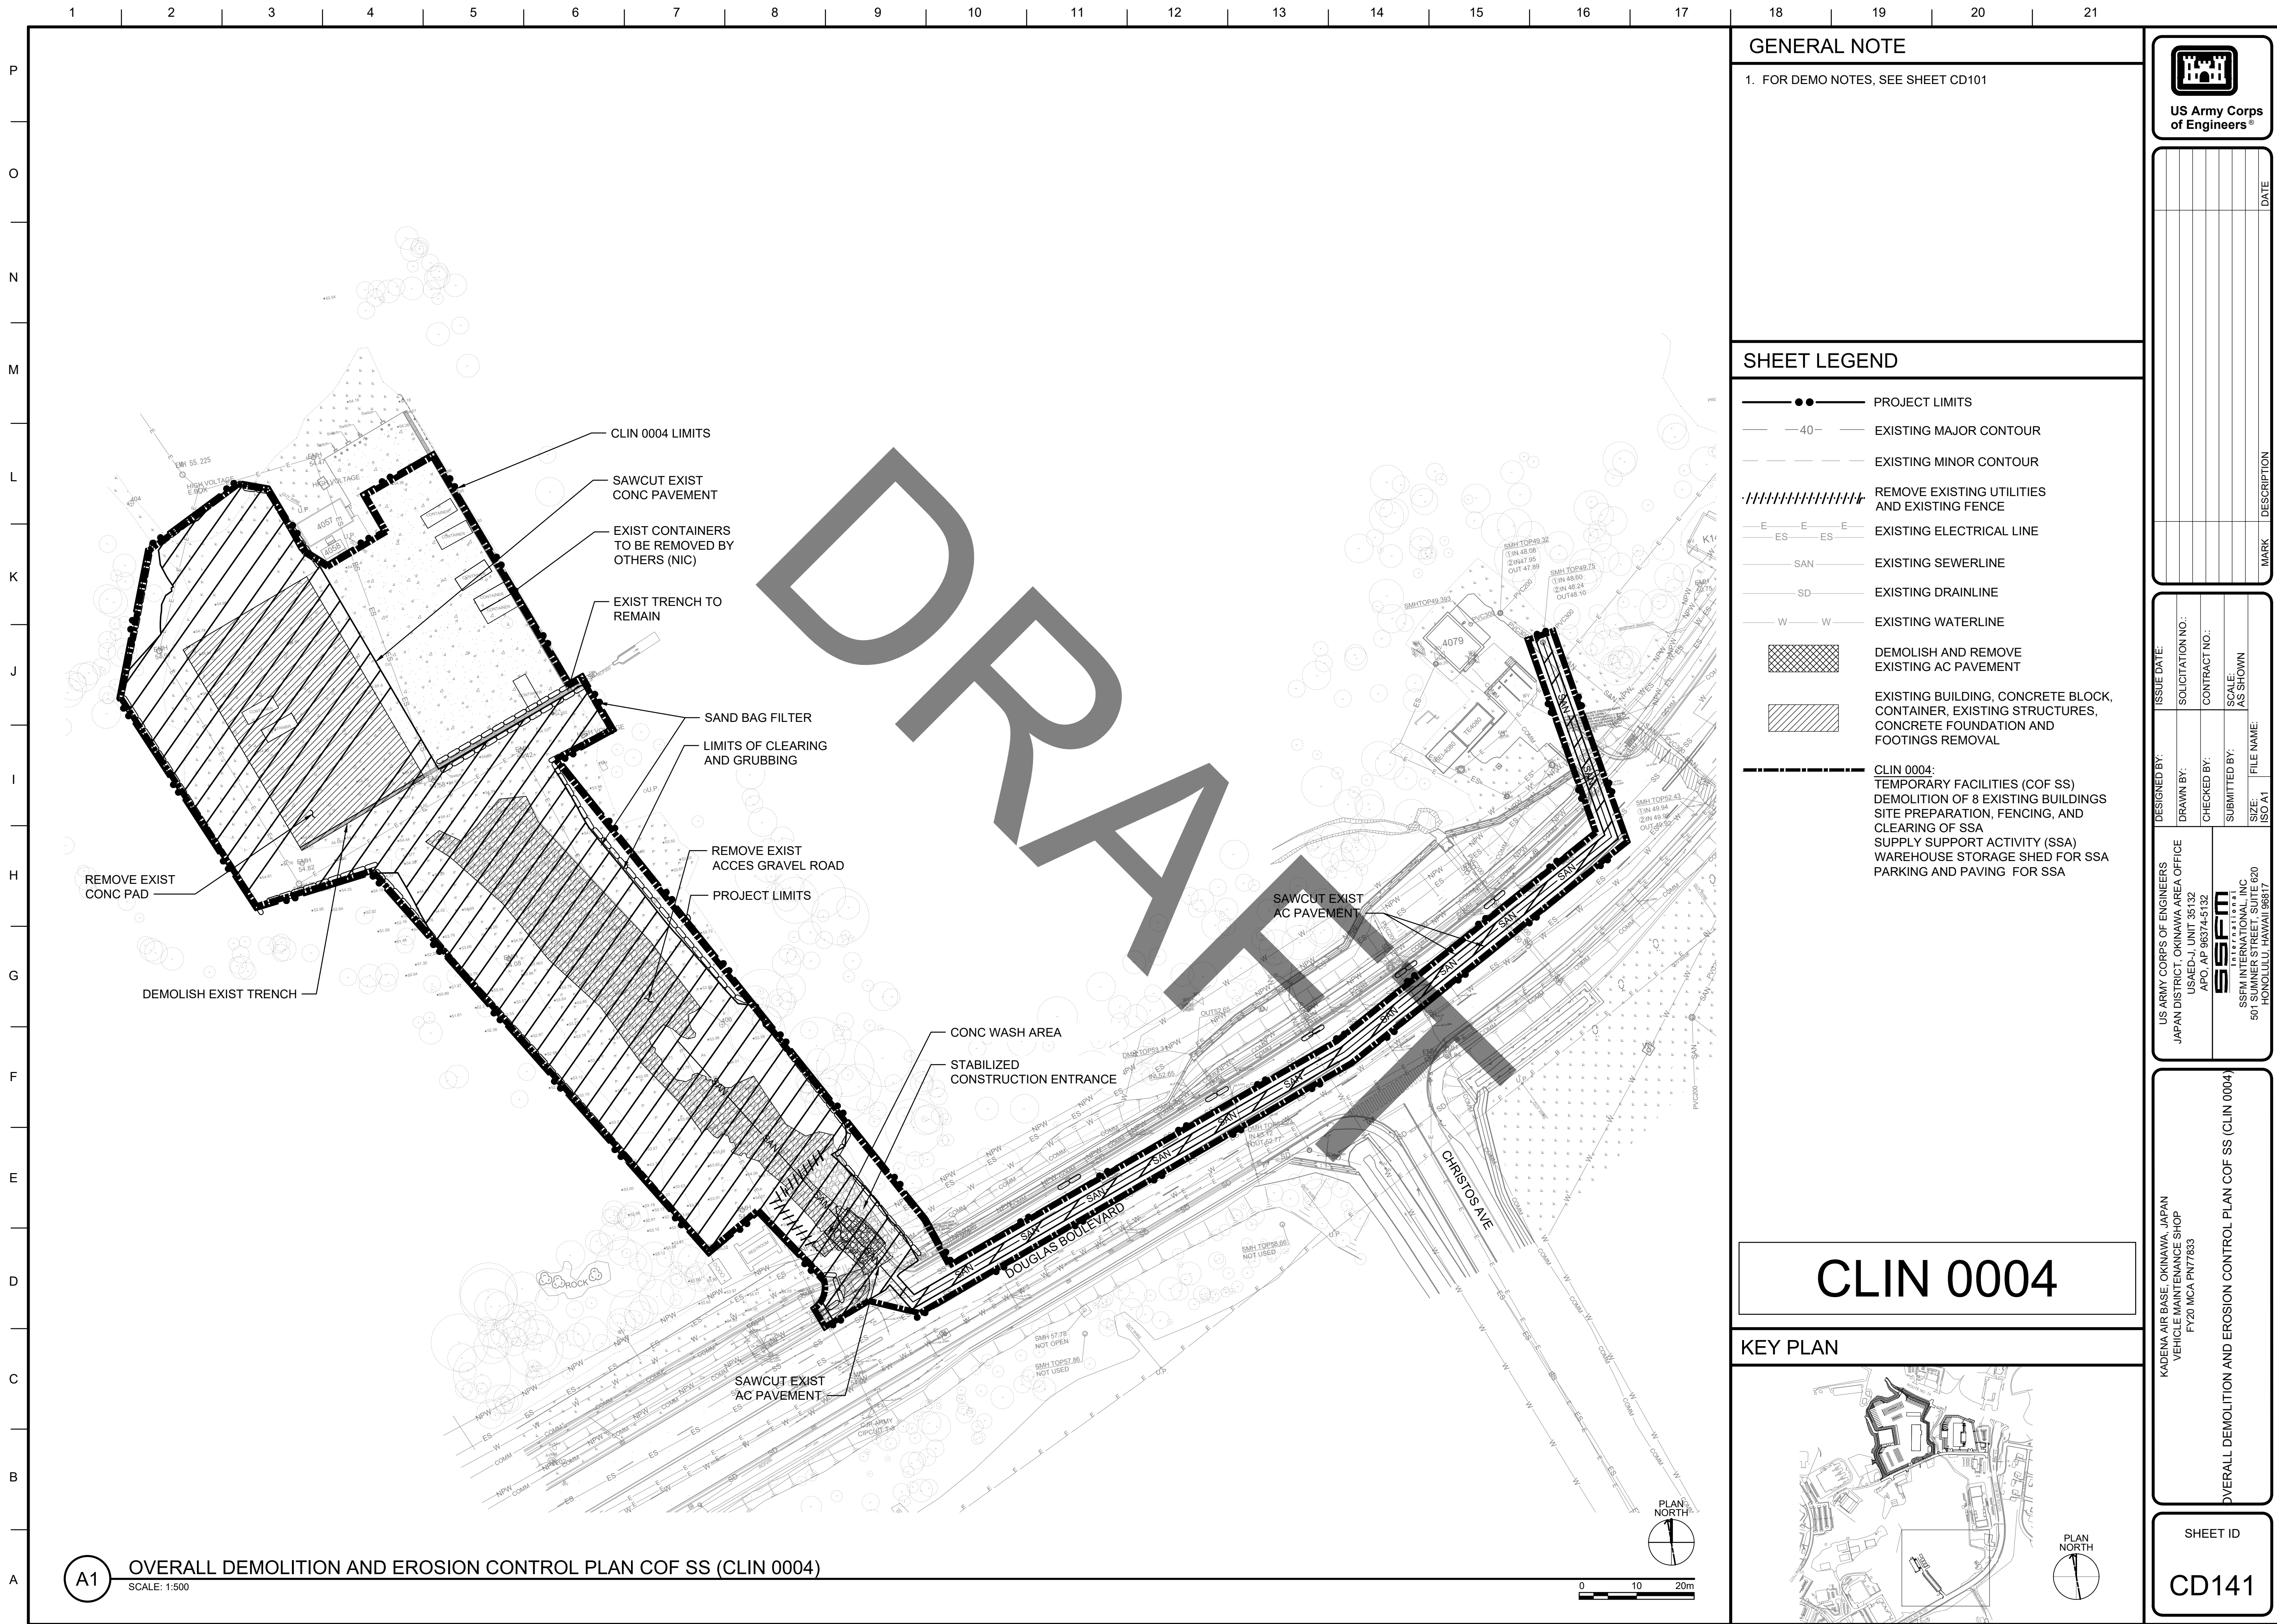

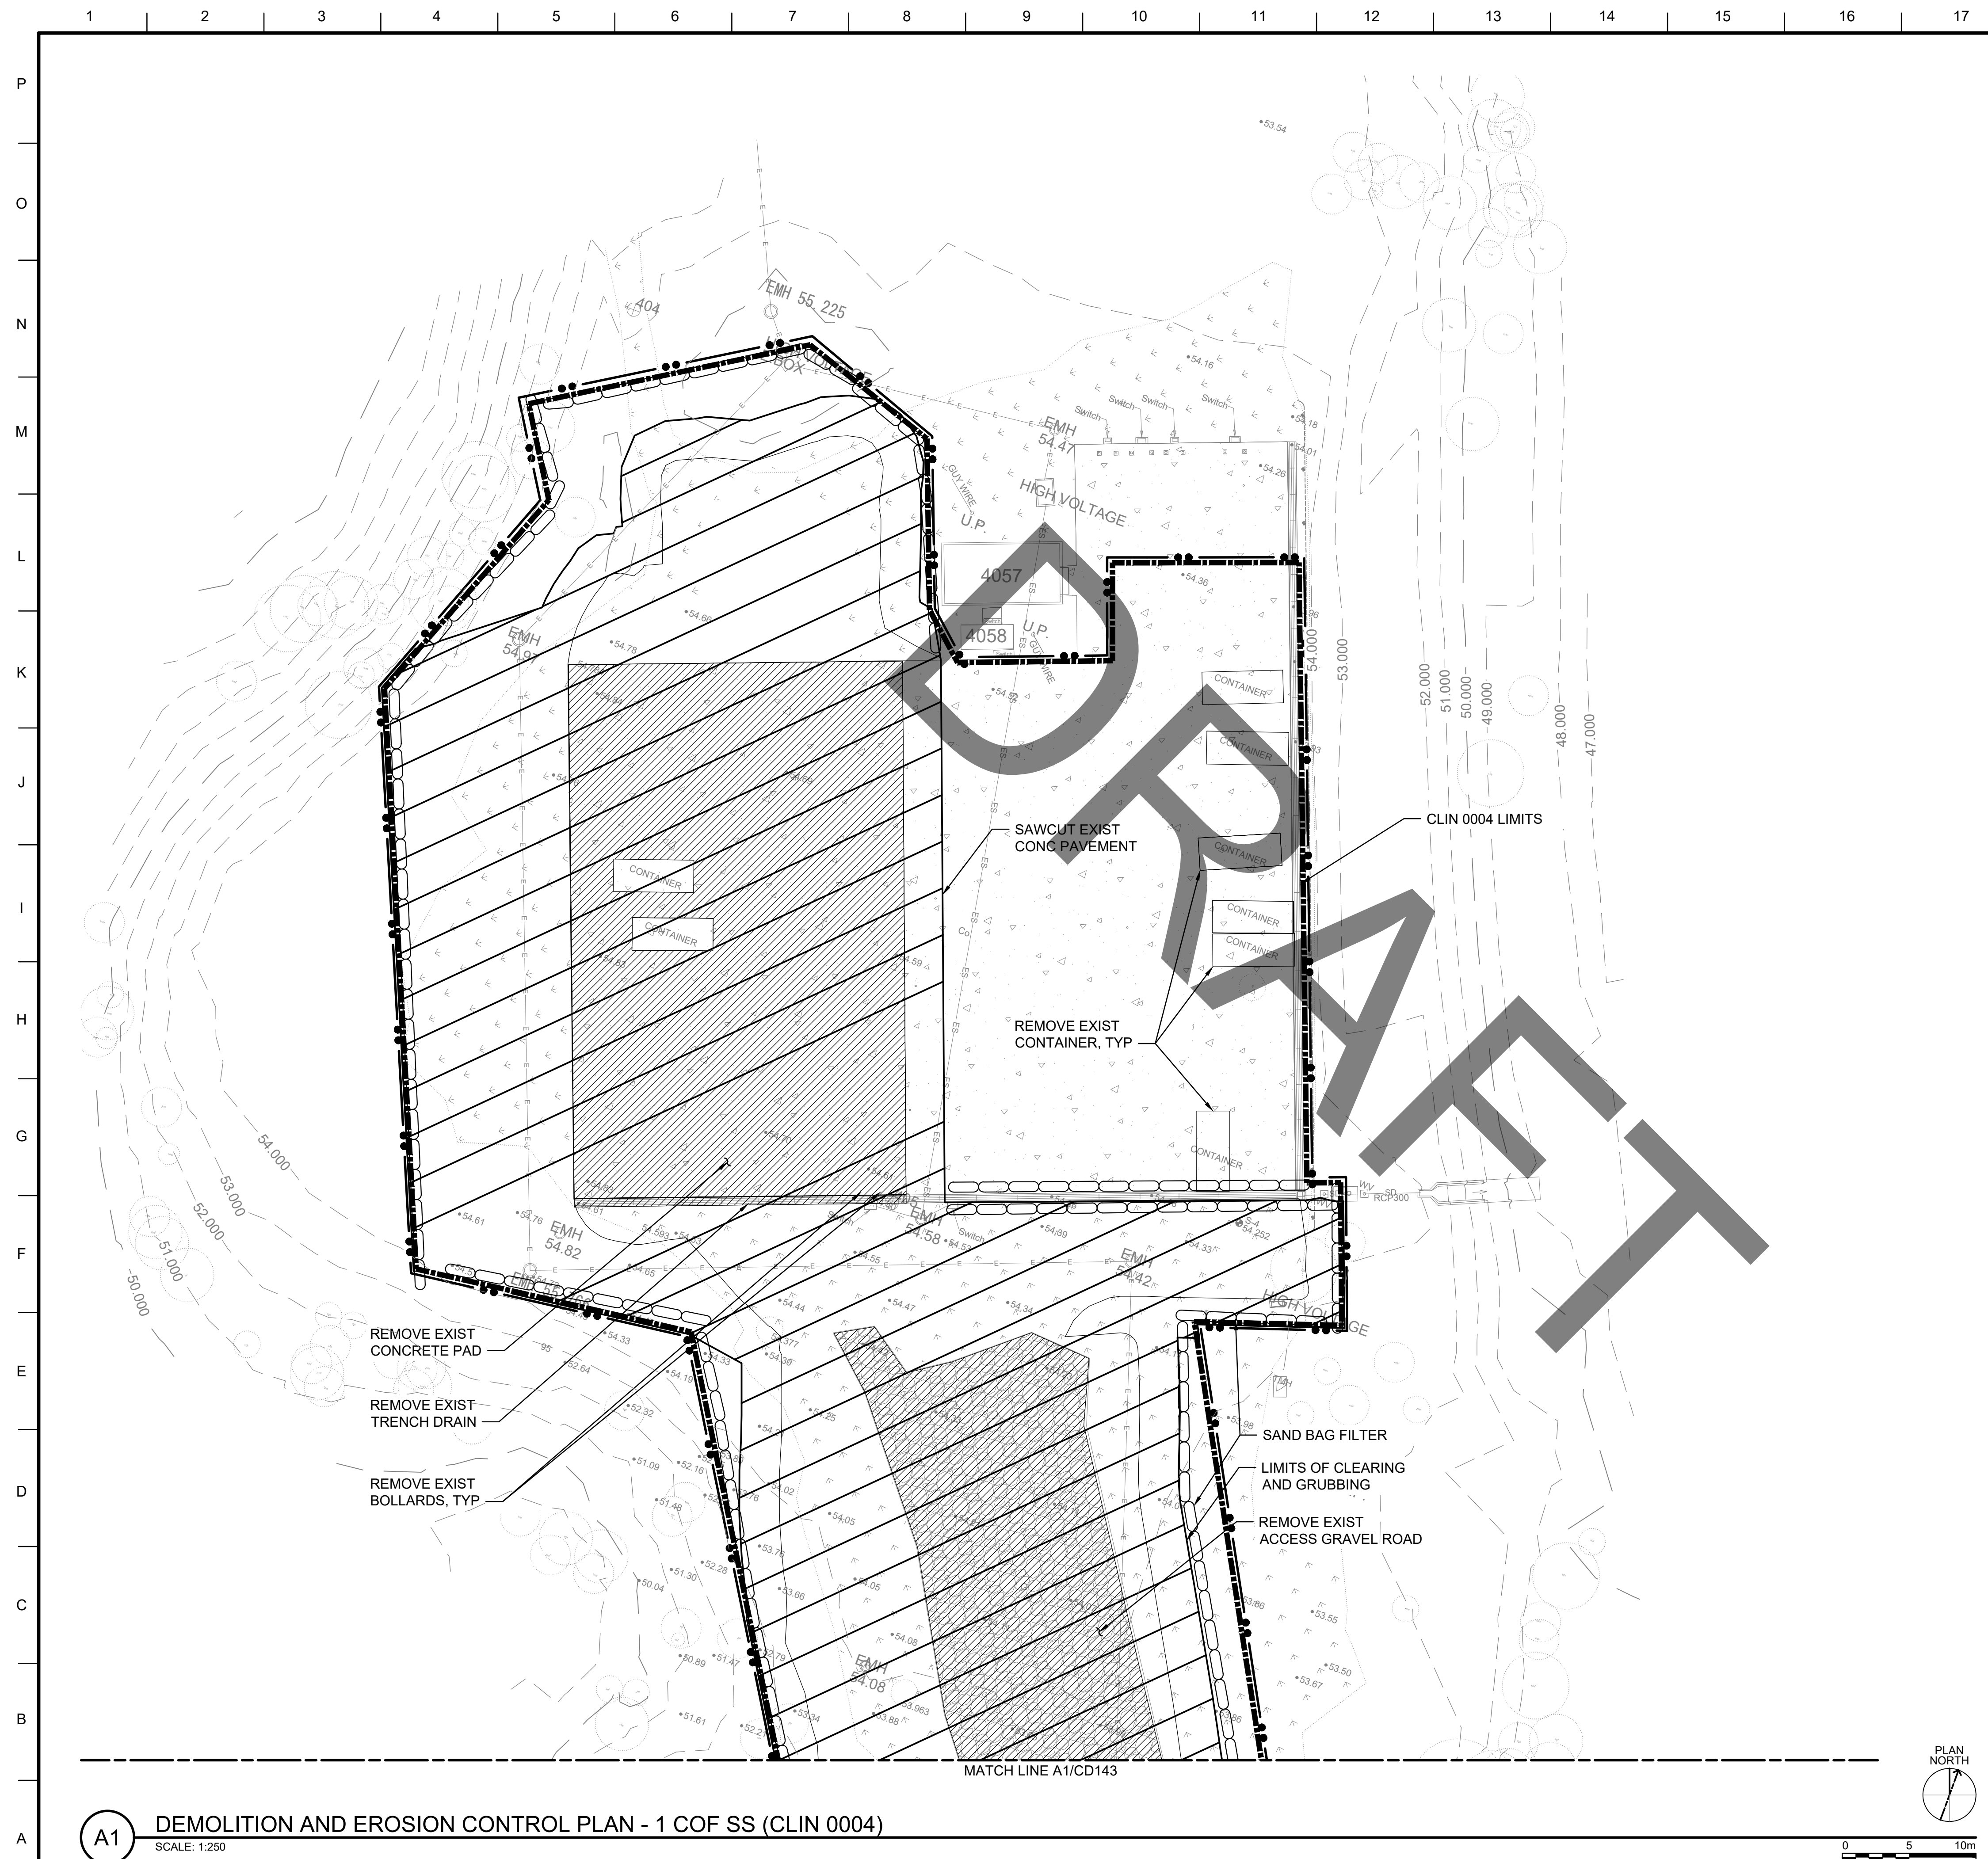



GENERAL NOTE

1. FOR DEMO NOTES, SEE SHEET CD101




**U.S. Army Corps
Engineers®**

SHEET LEGEND

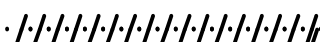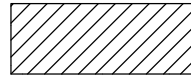- | | |
|---|---|
|  | PROJECT LIMITS |
|  | EXISTING MAJOR CONTOUR |
|  | EXISTING MINOR CONTOUR |
|  | REMOVE EXISTING UTILITIES
AND EXISTING FENCE |
|  | EXISTING ELECTRICAL LINE |
|  | EXISTING SEWERLINE |
|  | EXISTING DRAINLINE |
|  | EXISTING WATERLINE |
|  | DEMOLISH AND REMOVE
EXISTING AC PAVEMENT |
|  | DEMOLISH AND REMOVE
EXISTING BUILDING, CONCRETE BLOCK,
CONTAINER, EXISTING STRUCTURES,
CONCRETE FOUNDATION AND
FOOTINGS REMOVAL |
|  | CLIN 0004:
TEMPORARY FACILITIES (COF SS)
DEMOLITION OF 8 EXISTING BUILDINGS
SITE PREPARATION, FENCING, AND
CLEARING OF SSA
SUPPLY SUPPORT ACTIVITY (SSA)
WAREHOUSE STORAGE SHED FOR SSA
PARKING AND PAVING FOR SSA |

KEY PLAN

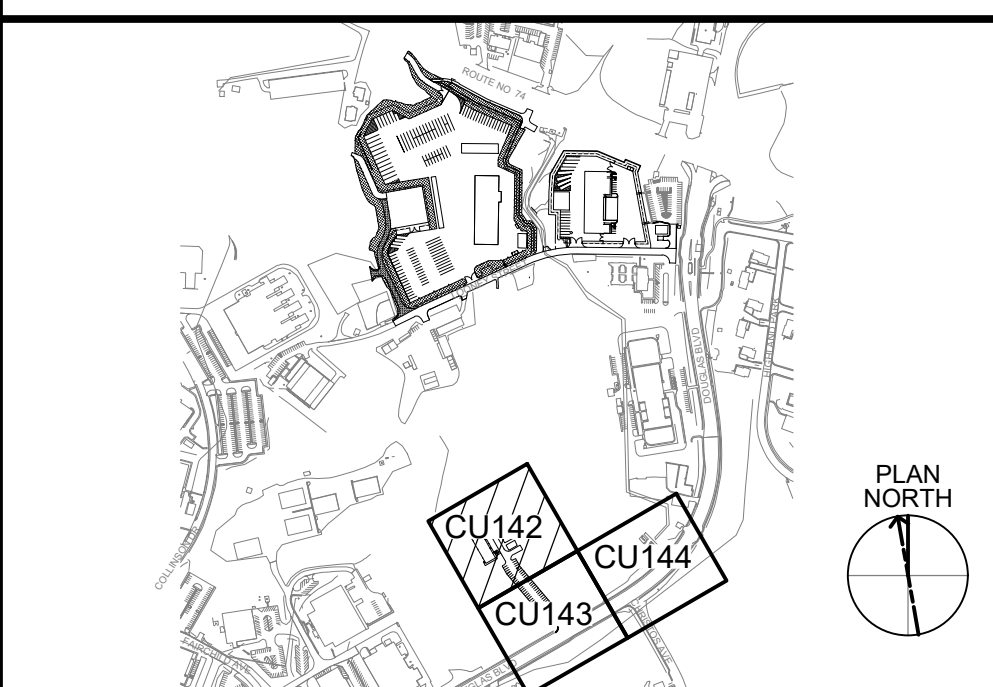

ORDER NO.: ORDER DATE: ORDER BY:	CONTRACT NO.: SCALE: AS SHOWN
DRAWING NO.: DRAWN BY:	SUBMITTED BY:
CHECKED BY:	FILE NAME:
SIZE:	ISO A1




SSFM INTERNATIONAL, INC
 501 SUMMER STREET, SUITE 620
 HONOLULU, HAWAII 96817

USAED-J, UNIT 35132
 APO, AF 96374-5132

FY20 MCA PN77833

SHEET ID
CD142

INTERMEDIATE DESIGN

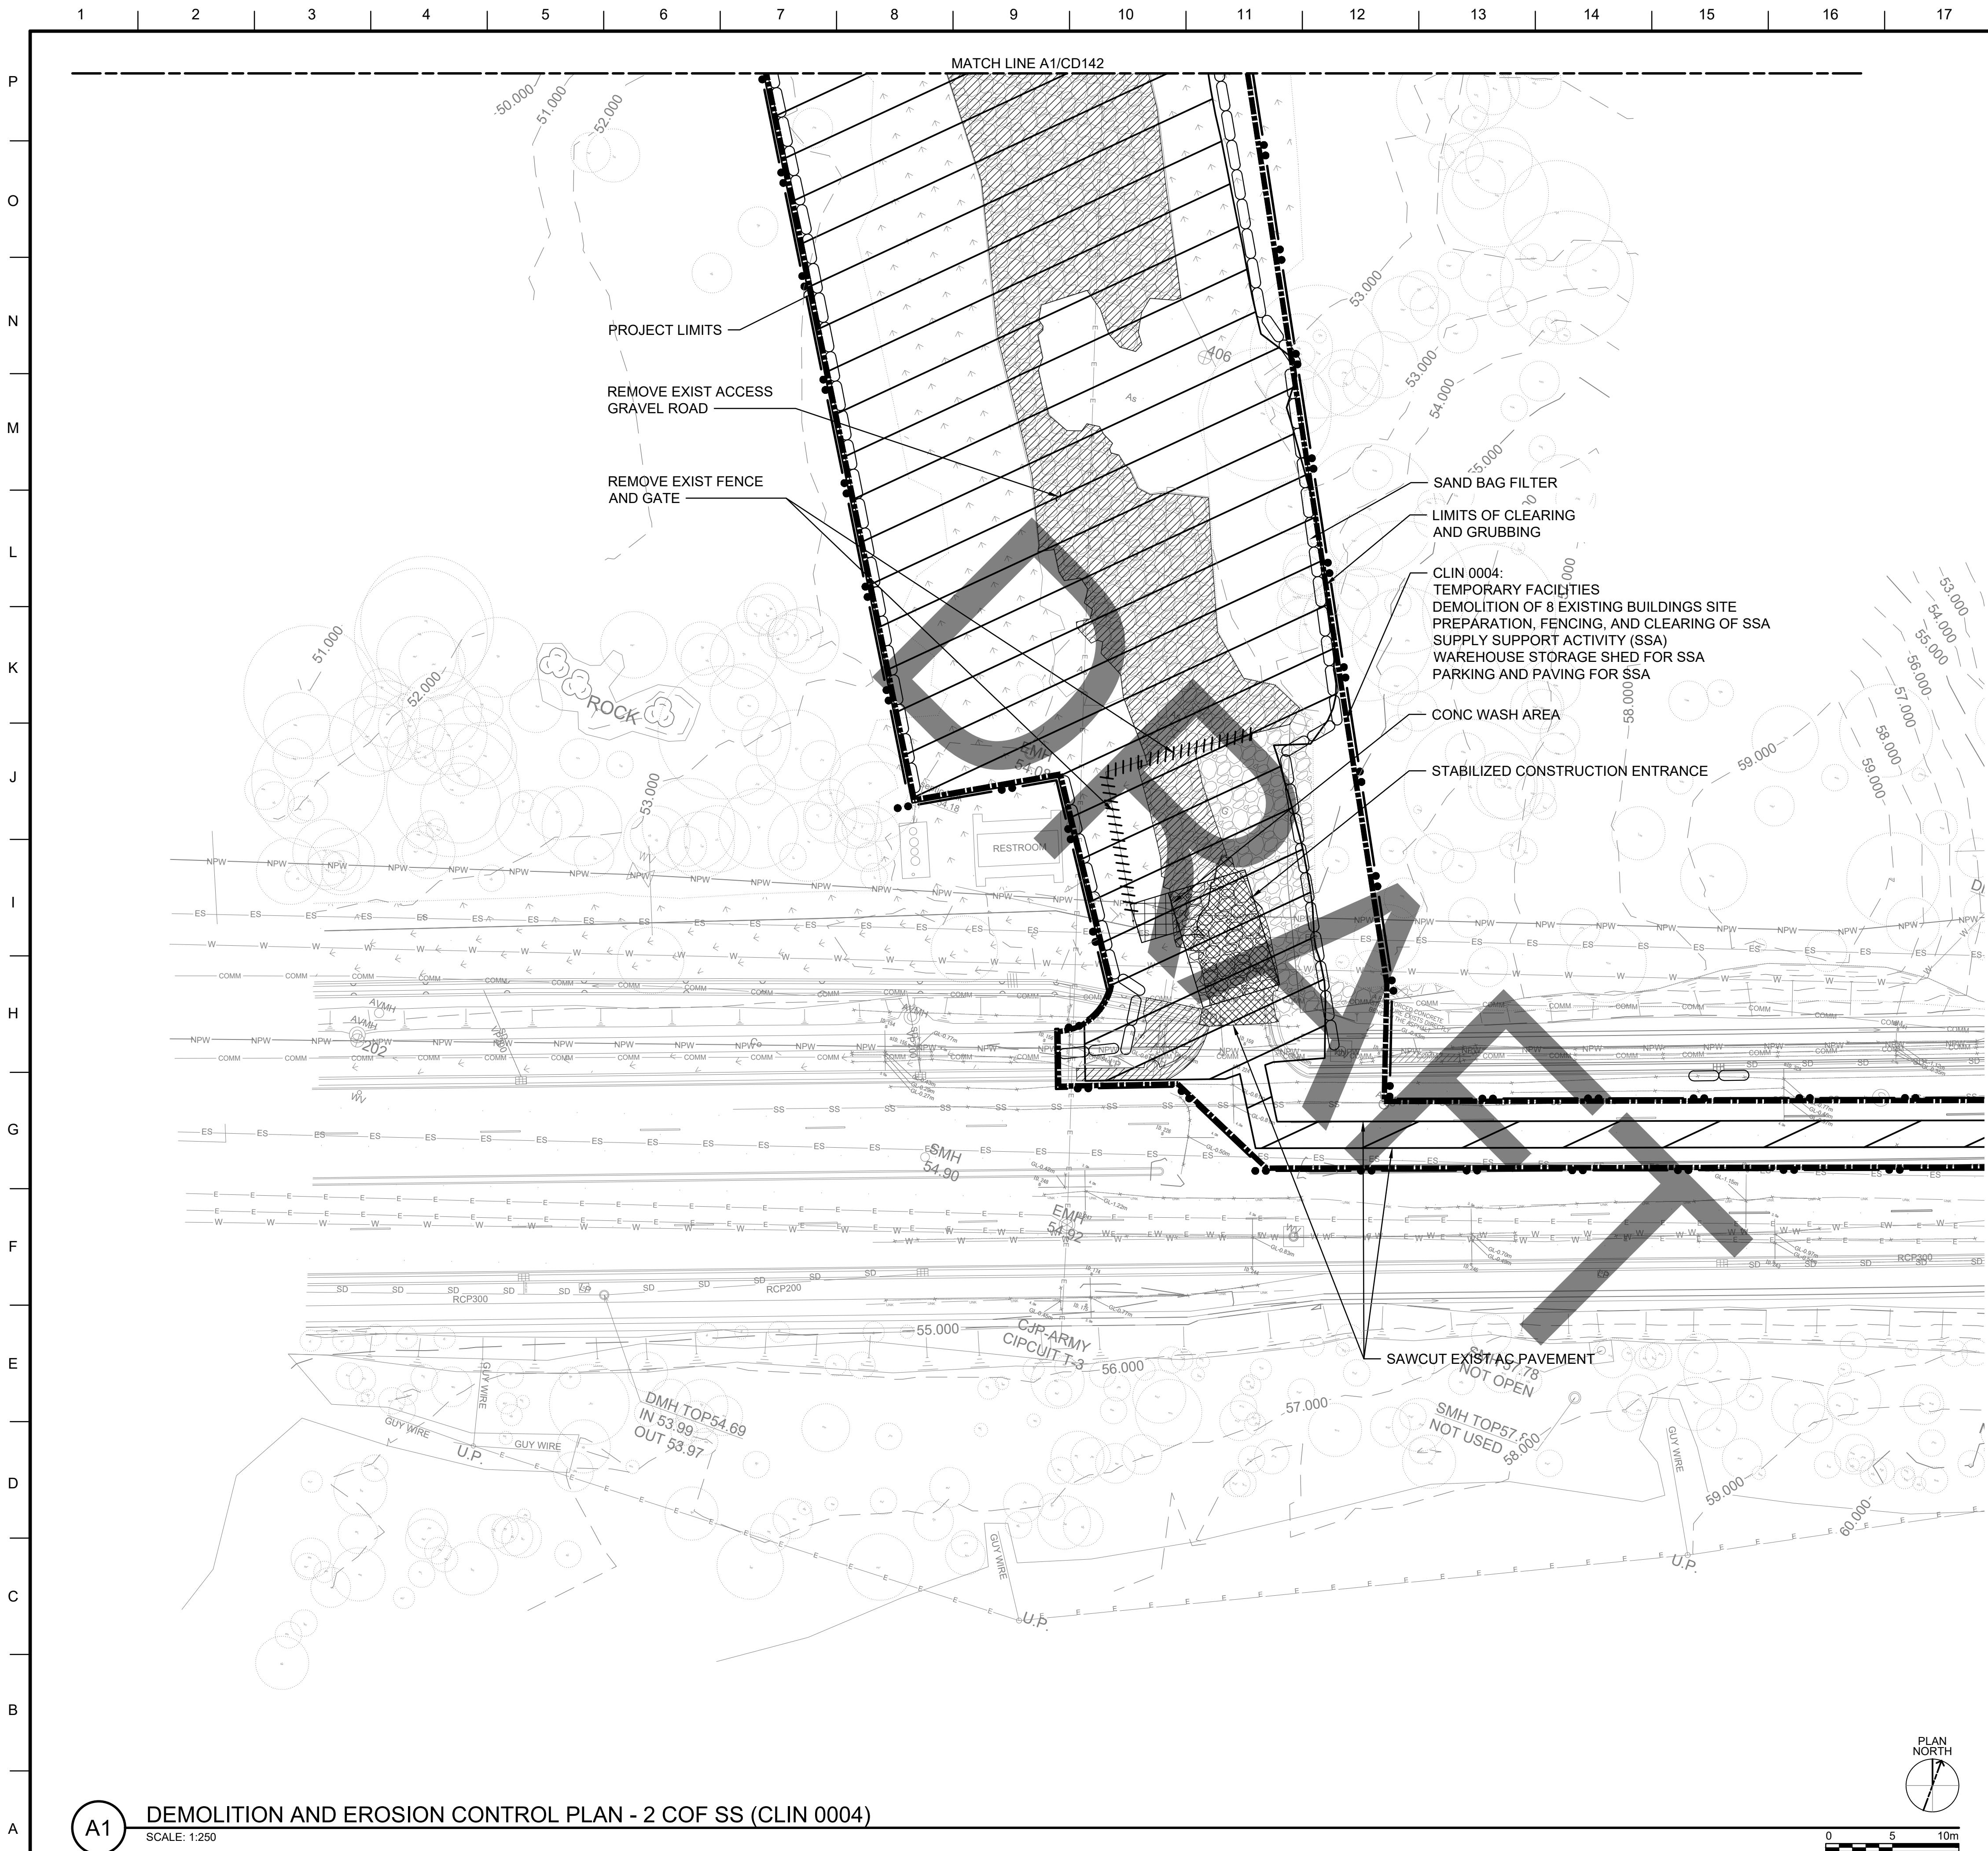

GENERAL NOTE


1. FOR DEMO NOTES, SEE SHEET CD101

SHEET LEGEND

- PROJECT LIMITS
- EXISTING MAJOR CONTOUR
- EXISTING MINOR CONTOUR
- REMOVE EXISTING UTILITIES AND EXISTING FENCE
- EXISTING ELECTRICAL LINE
- EXISTING SEWERLINE
- EXISTING DRAINLINE
- EXISTING WATERLINE
- DEMOLISH AND REMOVE EXISTING AC PAVEMENT
- EXISTING BUILDING, CONCRETE BLOCK, CONTAINER, EXISTING STRUCTURES, CONCRETE FOUNDATION AND FOOTINGS REMOVAL
- CLIN 0004: TEMPORARY FACILITIES (COF SS) DEMOLITION OF 8 EXISTING BUILDINGS SITE PREPARATION, FENCING, AND CLEARING OF SSA SUPPLY SUPPORT ACTIVITY (SSA) WAREHOUSE STORAGE SHED FOR SSA PARKING AND PAVING FOR SSA

CLIN 0004

KEY PLAN

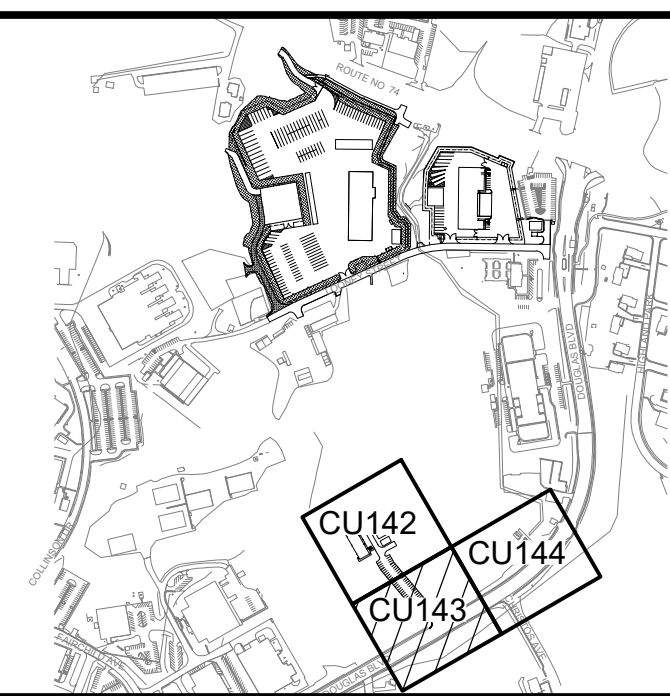

US Army Corps of Engineers

ISSUE DATE:		SOLICITATION NO.:		CONTRACT NO.:	
DESIGNED BY:	DRAWN BY:	CHECKED BY:	SUBMITTED BY:	SCALE:	AS SHOWN
US ARMY CORPS OF ENGINEERS JAPAN DISTRICT, OKINAWA AREA OFFICE USAD-J UNIT 35132 APO AP 96374-5132		SSEM INTERNATIONAL, INC. 501 SUMNER STREET, SUITE 620 HONOLULU, HAWAII 96817		FILE NAME:	ISO A1

KADENA AIR BASE, OKINAWA, JAPAN
VEHICLE MAINTENANCE SHOP
FY20 MCA PN77833

DEMOLITION AND EROSION CONTROL PLAN - 2 COF SS (CLIN 0004)

SHEET ID

CD143

INTERMEDIATE DESIGN