

P
O
N
M
L
K
J
I
H
G
F
E
D
C
B
A

DUCT CABLE SCHEDULE				
TAG	DUCTS	CABLES		
(a)	(6) 104mm (4) 104mm 345'	48S08F F.O.LINK10-9-1-48 BLDG926TOBLDG4065 P6-24FF 12S08F F.O.LINK10-7B-1-12 BLDG973TOBLDG52200 P12-22PLAP CAJ20-1-1200 24S10F F.O.LINK4-1-12+ A.13-24 TMH510TOBLDG6105 12S08F F.O.LINK10-5A-1-6+ A.7-12 BLDG4081TOGATE3	P2-22PLAP CA45-1-200 P6-24FF FA09-1-87+ 151-300+ 401-600+ A.301-400+ B.88-100+ C.101-150 CATV U.S.NAVY (N)12SM B3670-B6105 F.O.LINK BLDG4044: 13-144+1-12DD	P6-24FF CA07-176-600+ P6-24FF CA07-176-600+ A.1-175
(b)	(3) 104mm 101'	48S08F F.O.LINK10-9-1-48 BLDG926TOBLDG4065 P50-24FF CA09-501-550		
(c)	(4) 104mm 191'	144SM FOC FROM B718 F.O.LINK B4040, 13-144(+1-12DD) 12SM FOC FR B4040 F.O.LINK B4045 12SM FOC FR B4040 F.O.LINK B4047	12SM FOC FR B4040 F.O.LINK B4046 P50-24FF CA07-176-200+ S.26-50 P50-24FF CA07-201-225+ A.26-50	P50-24FF CA07-226-250+ A.26-50 144SM FOC B4040-TMH510
(d)	(4) 104mm 28'	12SM FOC FR B4040 F.O.LINK B4044 36SM FOC FR B4040 F.O.LINK B4045, B4046,B4047 144SM FOC FROM B718 F.O.LINK B4040, 13-144(+1-12DD)	P50-24FF CA07-251-275+ A.26-50 P50-24FF CA07-276-300+ A.26-50 P50-24FF CA07-301-325+ A.26-50	P50-24FF CA07-326-350+ A.26-50 144SM FOC B4040-TMH510
(e)	(4) 104mm 23'	12SM FOC FR B4040 F.O.LINK B4041 12SM FOC FR B4040 F.O.LINK B4042 12SM FOC FR B4040 F.O.LINK B4043	P50-24FF CA07-301-325+ S.26-50 P50-24FF CA07-276-300+ A.26-50 P50-24FF CA07-326-350+ A.26-50	
(f)	(2) 104mm 105'	12SM FOC FR B4040 F.O.LINK B4045 12SM FOC FR B4040 F.O.LINK B4047 12SM FOC FR B4040 F.O.LINK B4046	P50-24FF CA07-176-200+ S.26-50 P50-24FF CA07-201-225+ A.26-50 P50-24FF CA07-226-250+ A.26-50	
(g)	(4) 104mm 225'	FROM BLDG 718 FO LINK B4044: 12-114+1-12DD P6-24FF CA07-176-600+ A.1-175	144SM FOC B4040-TMH510 53115-4040, 01-96	
(h)		12S08F F.O. LINK10-5B-1-6+ A.7-12 BLDG4081TOGATE3 P25-24FF CA09-63-87	CA45-176-181 12L8.3F FO 926-4069,49-60	
(i)	(6) 104mm 347' TO (E)TMH-624	P12-22PEC CAJ20-1-975+ 1001-1200+ A.976-1000 12S08F F.O.LINK10-7B-1-12 BLDG973TOBLDG52200 12S08F F.O.LINK10-5A-1-6+ A.7-12 BLDG4081TOBLDG533115 CATV	24S10FN2 F.O.LINK4-1-12+ A.13-24 P2-24PF CA45-1-200 U.S.NAVY (N)12SM B3670-B6105	
(j)	(2) 104mm 363' TO (E)TMH-223- 26-A	46L8.3F FO 926-6105,1-36+ FO 926-52200,34-48 144SM FOC B4040-TMH510		
(k)	(4) 104mm 70'	P6-24FF CA09-1-62+ 151-300+ 401-600+ A.301-400+ B.88-100+ C.101-150+ D.63-87	P25-24FF CAJ20-976-1000 48S08F F.O.LINK10-9-1-48 BLDG926TOBLDG4065	
(l)	(2) 104mm	48 STRD SM FO TMH520 - PEDESTALS		
(m)	(1) 104mm	48 STRD SM FO TMH520 - PEDESTALS		



GENERAL NOTES

1. SEE CIVIL AND ELECTRICAL PLANS FOR SITE DEMOLITION WORK AND CLOSELY COORDINATE THE DEMOLITION WORK FOR TELECOMMUNICATIONS SYSTEMS.
2. PRIOR TO ANY TELECOMMUNICATIONS INFRASTRUCTURE AND CABLE DEMOLITION WORK, ENSURE THAT THE NEW INFRASTRUCTURE AND CABLES ARE ESTABLISHED TO MINIMIZE DISRUPTION TO THE OPERATIONS OF THE EXISTING FACILITIES.
3. THE CONTRACTOR SHALL BE RESPONSIBLE TO SUBMIT A PROPOSED PHASING SCHEME IN COORDINATION WITH CIVIL AND ELECTRICAL WORK FOR REVIEW AND APPROVAL PRIOR TO START OF DEMOLITION WORK.

KEY NOTES

1. REMOVE ALL EXIST FO AND COPPER CABLES SERVING ADA BUILDINGS BACK TO CABLE HUT, INCLUDING THE ASSOCIATED INFRASTRUCTURE.
2. EXISTING MAINTENANCE HOLES SHALL BE REMOVED. COORDINATE THE REMOVAL OF MAINTENANCE HOLES WITH THE CIVIL WORK.

CLIN 0004

- CLIN 0004
- CONSTRUCTINO OF TEMPORARY FACILITIES AT SWING SPACE SITE MUST BE COMPLETED PRIOR TO DEMOLITION OF EXISTING ADA BUILDINGS (B4040 THRU B4047) AND SITE PREPARATION WORK FOR SSA FACILITIES.
 - CONSTRUCTION OF NEW SUPPLY SUPPORT ACTIVITY (SSA) WAREHOUSE, STORAGE SHED AND ASSOCIATED TELECOMMUNICATIONS INFRASTRUCTURE.
 - CONSTRUCTION OF SSA PARKING LOT.



US Army Corps
of Engineers®

MARK	DESCRIPTION	DATE

DESIGNED BY:	ISSUE DATE:
DRAWN BY:	SOLICITATION NO.:
CHECKED BY:	CONTRACT NO.:
SUBMITTED BY:	SCALE:
SIZE:	FILE NAME:
ISO A1	AS SHOWN
US ARMY CORPS OF ENGINEERS JAPAN DISTRICT, OKINAWA AREA OFFICE USAED-J UNIT 35132 APO, AP 96374-5132 SSFM SSFM INTERNATIONAL, INC. 501 SUMNER STREET, SUITE 620 HONOLULU, HAWAII 96817	

KADENA AIR BASE, OKINAWA, JAPAN VEHICLE MAINTENANCE SHOP FY20 MCA PN77833 PARTIAL SITE TELECOM DEMOLITION PLAN (CLIN 0004)


SHEET ID

TS132

INTERMEDIATE DESIGN


(A1) PARTIAL SITE TELECOMMUNICATION DEMOLITION PLAN (CLIN0004)

1:500

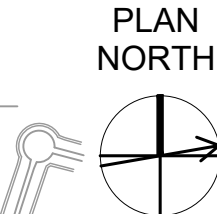

0 20 40m
SCALE: 1:500

P —
 O —
 N —
 M —
 L —
 K —
 J —
 I —
 H —
 G —
 F —
 E —
 D —
 C —
 B —
 A

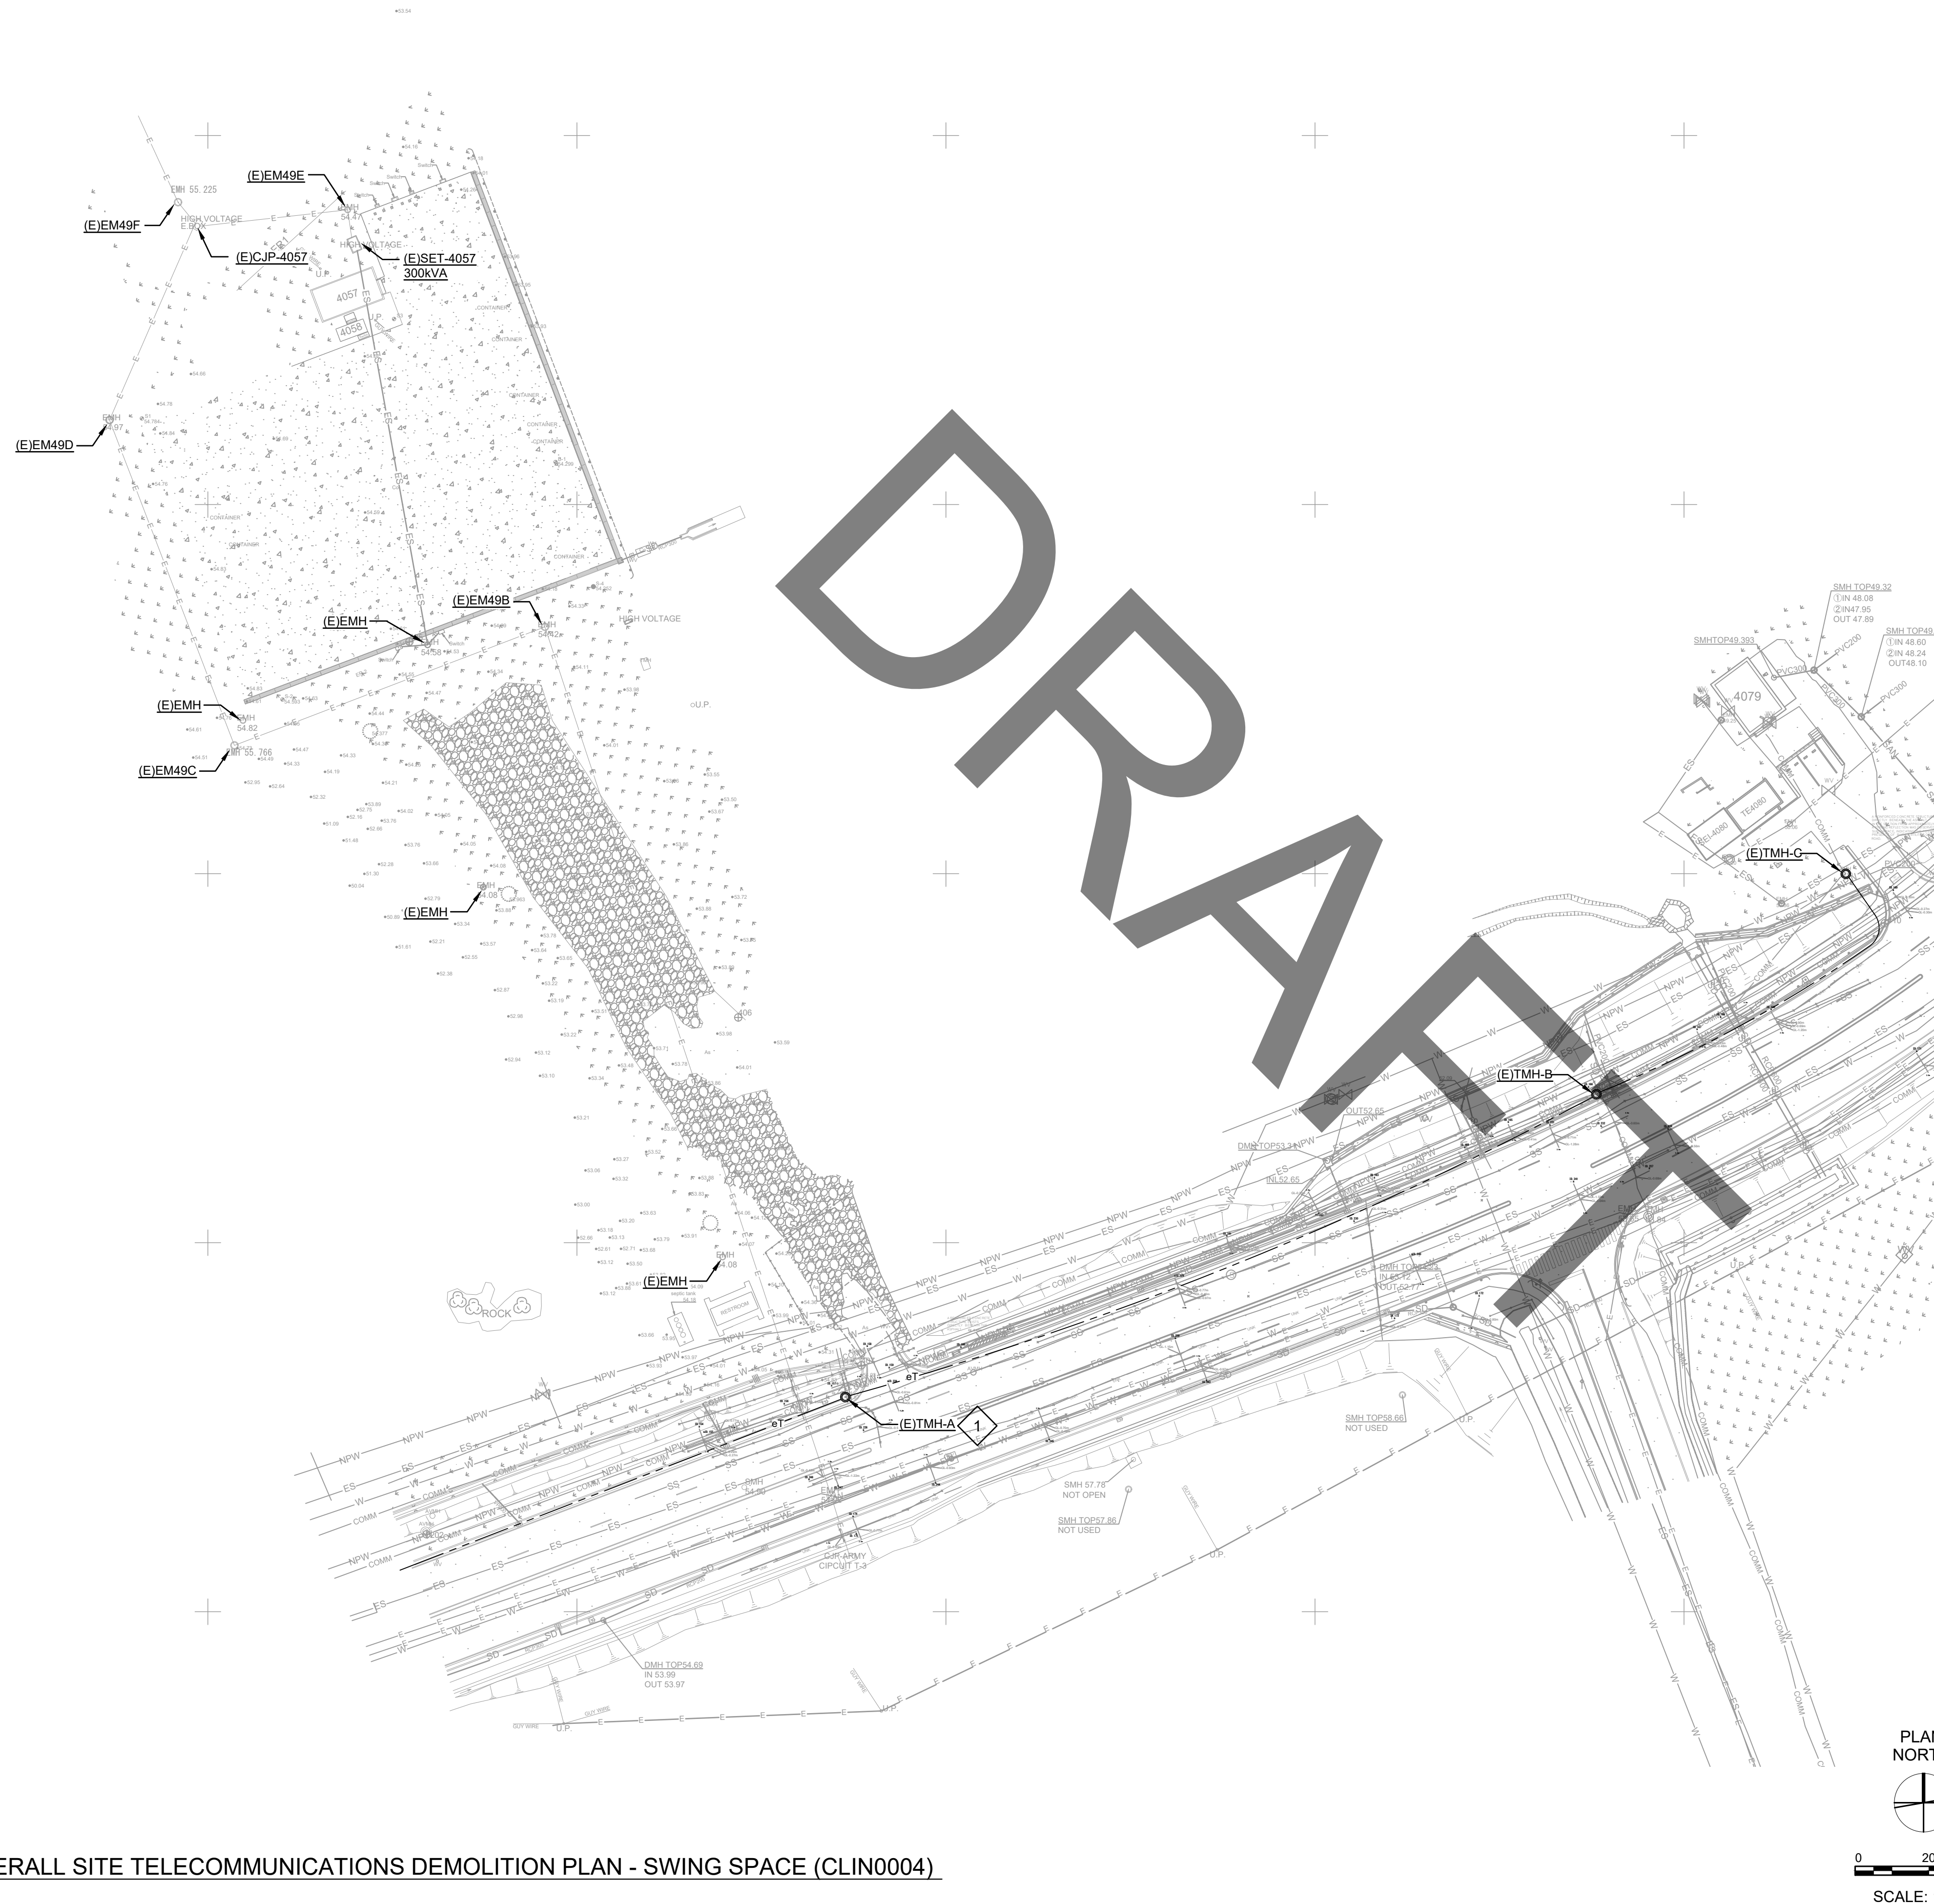

GENERAL NOTES

1. SEE CIVIL AND ELECTRICAL PLANS FOR SITE DEMOLITION WORK AND CLOSELY COORDINATE THE DEMOLITION WORK FOR TELECOMMUNICATIONS SYSTEMS.
2. PRIOR TO ANY TELECOMMUNICATIONS INFRASTRUCTURE AND CABLE DEMOLITION WORK, ENSURE THAT THE NEW INFRASTRUCTURE AND CABLES ARE ESTABLISHED TO MINIMIZE DISRUPTION TO THE OPERATIONS OF THE EXISTING FACILITIES.
3. THE CONTRACTOR SHALL BE RESPONSIBLE TO SUBMIT A PROPOSED PHASING SCHEME IN COORDINATION WITH CIVIL AND ELECTRICAL WORK FOR REVIEW AND APPROVAL PRIOR TO START OF DEMOLITION WORK.




**U.S. Army Corps
Engineers®**

KEY NOTES

- 1 EXISTING MAINTENANCE HOLE SHALL BE SALVAGED AND REUSED. MODIFIED MAINTENANCE HOLE FINISH TO MATCH THE THE FINAL GRADING.

[illegible]

 
JAPAN DISTRICT, OKINAWA AREA OFFICE USJED-1, UNIT 35132 APO, AP 96374-5132	 SSFM INTERNATIONAL, INC 501 SUMNER STREET, SUITE 620 HONOLULU, HAWAII 96817	DRAWN BY: CHECKED BY: SUBMITTED BY: SOLICITATION NO.: CONTRACT NO.: SCALE: AS SHOWN
	SIZE	FILE NAME:
	ISO 1:1	

MAJENAT BASE, UNIKAWA, JAPAN
VEHICLE MAINTENANCE SHOP
FY20 MCA PN77833

SHEET ID

S141

INTERMEDIATE DESIGN

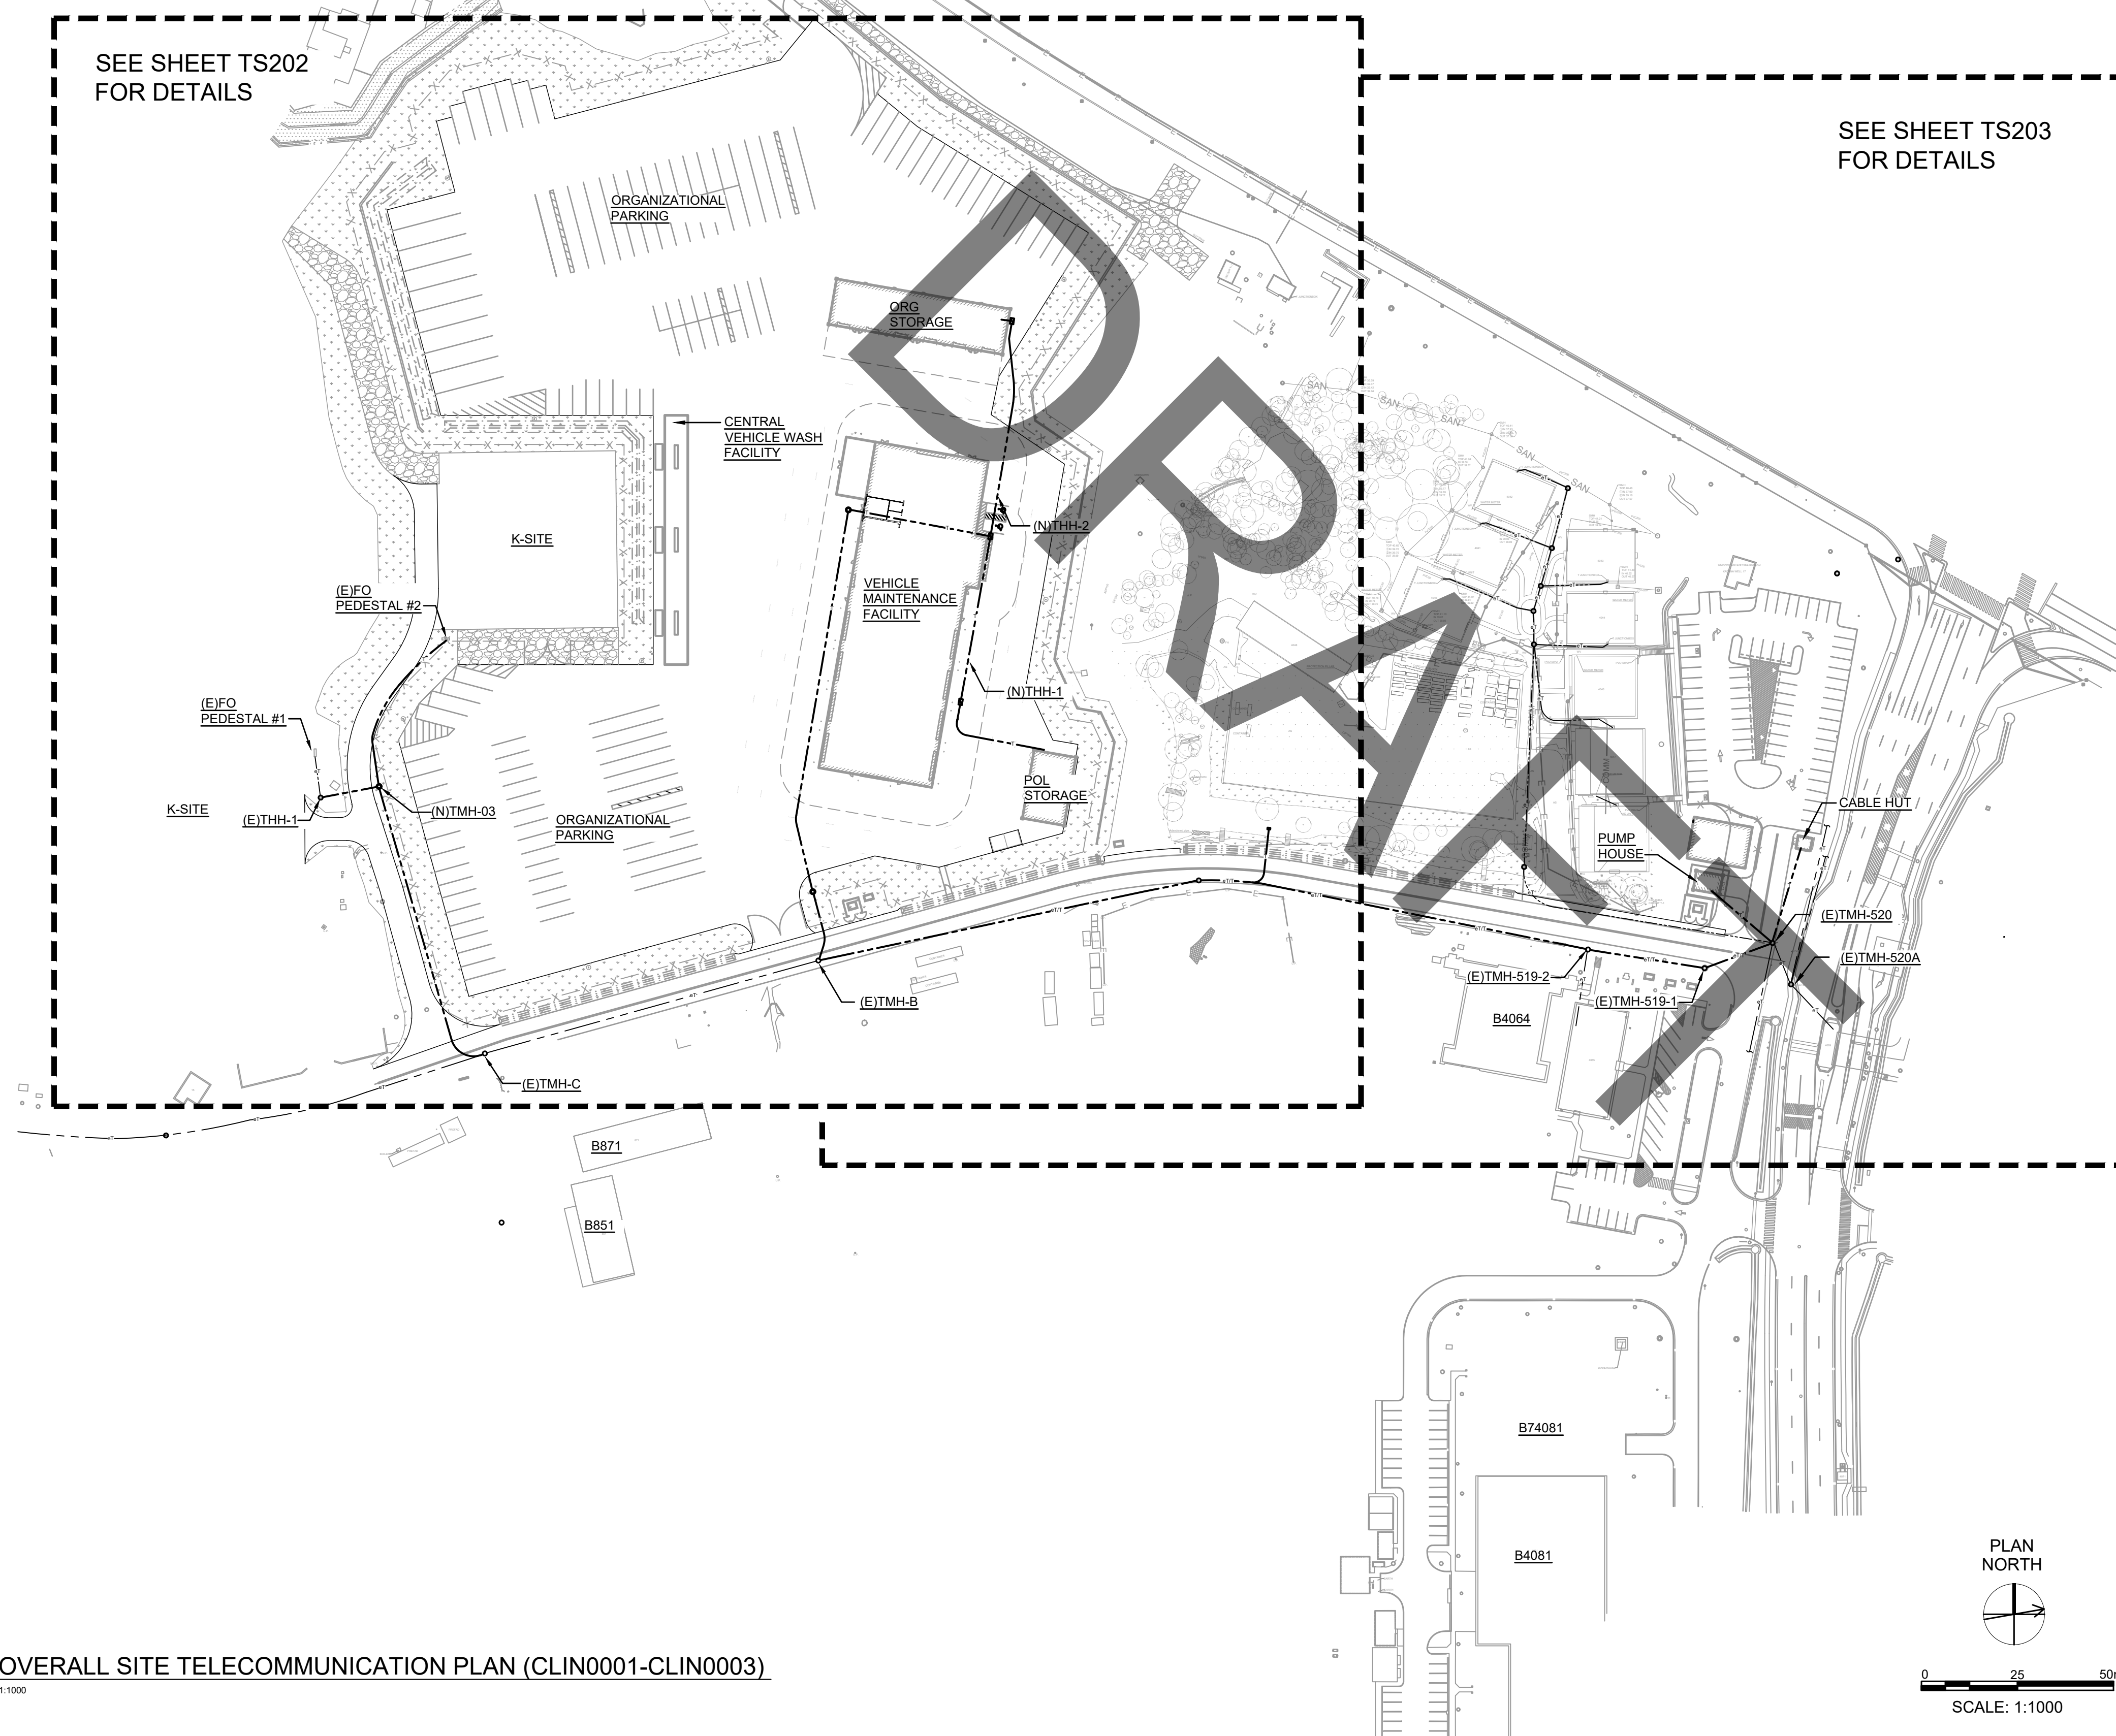

GENERAL NOTES

1. SEE CIVIL AND ELECTRICAL PLANS FOR SITE DEMOLITION WORK AND CLOSELY COORDINATE THE DEMOLITION WORK FOR TELECOMMUNICATIONS SYSTEMS.
2. PRIOR TO ANY TELECOMMUNICATIONS INFRASTRUCTURE AND CABLE DEMOLITION WORK, ENSURE THAT THE NEW INFRASTRUCTURE AND CABLES ARE ESTABLISHED TO MINIMIZE DISRUPTION TO THE OPERATIONS OF THE EXISTING FACILITIES.
3. THE CONTRACTOR SHALL BE RESPONSIBLE TO SUBMIT A PROPOSED PHASING SCHEME IN COORDINATION WITH CIVIL AND ELECTRICAL WORK FOR REVIEW AND APPROVAL PRIOR TO START OF DEMOLITION WORK.



US Army Corps
of Engineers®

[illegible]

KEY NOTES

UNCLASSIFIED DTI US ARMY CORPS OF ENGINEERS JAPAN DISTRICT, OKINAWA AREA OFFICE USAED-J, UNIT 35132 APO, AP 96374-5132		SSFM INTERNATIONAL, INC 501 SUMNER STREET, SUITE 620	UNCLASSIFIED DTI SOCIAL DATE:
	DRAWN BY:	CONSTRUCTION NO.:	SCALE: AS SHOWN
	CHECKED BY:	SUBMITTED BY:	FILE NAME:
	SIGNED BY:	DATE:	SIZE:

CLIN 0001-0003

CLIN 0001:

- SITE PREPARATION WORK FOR VMS FACILITIES.
- LOONEY STREET AND ELECTRICAL AND TELECOMMUNICATIONS INFRASTRUCTURE IMPROVEMENTS.
- CONSTRUCTION OF CABLE HUT, RELOCATION OF COMMUNICATIONS HUB FOR CRITICAL OPTICAL FIBER AND COPPER CABLES FROM B4040, AND REESTABLISH THE SERVICES.
- ENSURE THAT TELECOMMUNICATION SERVICES TO EXISTING ADA BUILDINGS (B4040 THRU B4047) ARE MAINTAINED.
- RESTORE OPTICAL FIBER CABLES TO K-SITES FROM NEW CABLE HUT.
- CONSTRUCTION OF VEHICLE MAINTENANCE SHOP, FIRE PUMP HOUSE, WATER STORAGE TANK, AND ASSOCIATED TELECOMMUNICATIONS INFRASTRUCTURE.

CLIN 0002:

- CONSTRUCTION OF ORGANIZATIONAL EQUIPMENT STORAGE, POL STORAGE, AND ASSOCIATED TELECOMMUNICATIONS INFRASTRUCTURE.


CLIN 0003:

- CONSTRUCTION OF ORGANIZATIONAL VEHICLE PARKING LOT.
- CONSTRUCTION OF WASH RACK.

KADENA AIR BASE, OKINAWA, JAPAN
VEHICLE MAINTENANCE SHOP
FY20 MCA PN77833

SHEET ID

TS201

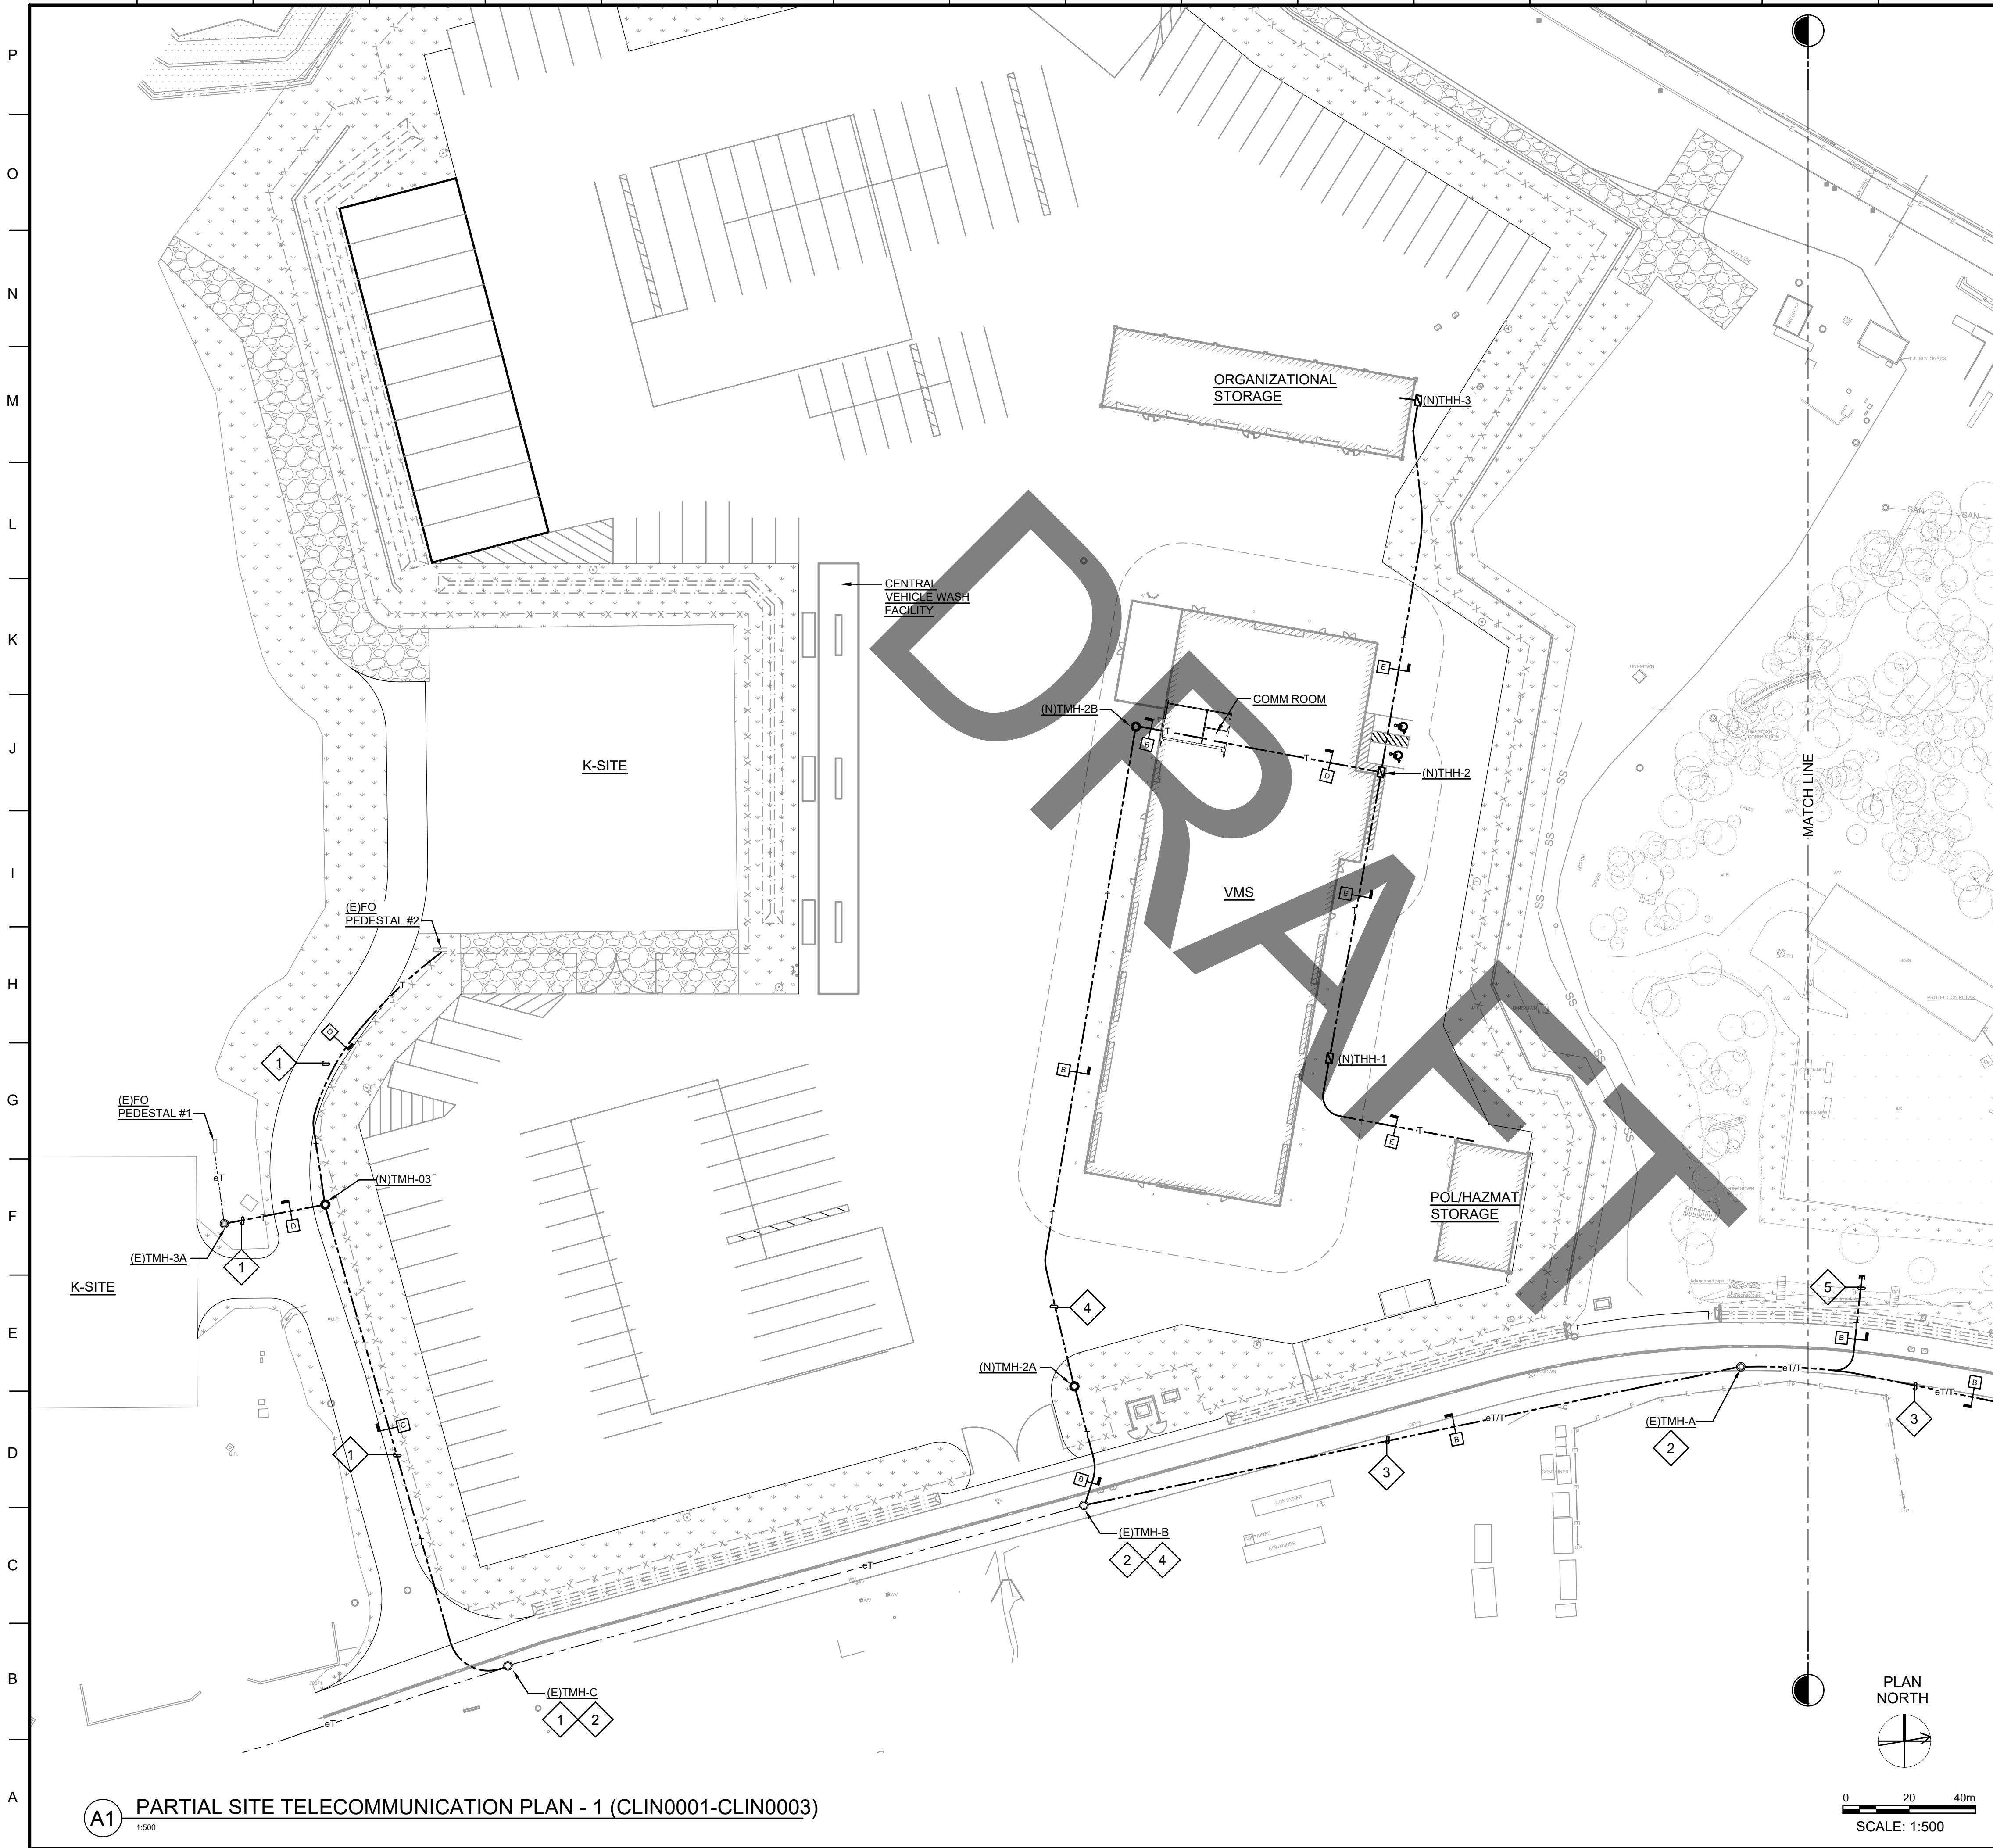

GENERAL NOTES

1. SEE CIVIL AND ELECTRICAL PLANS FOR SITE DEMOLITION WORK AND CLOSELY COORDINATE THE DEMOLITION WORK FOR TELECOMMUNICATIONS SYSTEMS.
2. PRIOR TO ANY TELECOMMUNICATIONS INFRASTRUCTURE AND CABLE DEMOLITION WORK, ENSURE THAT THE NEW INFRASTRUCTURE AND CABLES ARE ESTABLISHED TO MINIMIZE DISRUPTION TO THE OPERATIONS OF THE EXISTING FACILITIES.
3. THE CONTRACTOR SHALL BE RESPONSIBLE TO SUBMIT A PROPOSED PHASING SCHEME IN COORDINATION WITH CIVIL AND ELECTRICAL WORK FOR REVIEW AND APPROVAL PRIOR TO START OF DEMOLITION WORK.

KEY NOTES

1. EXTEND NEW DUCT LINES FROM (E)TMH-3 TO K-SITES TO RESTORE OPTICAL FIBER CABLE CONNECTIONS FROM NEW CABLE HUT TO FO PEDESTALS.
2. EXISTING MAINTENANCE HOLES AND DUCTS SHALL BE SALVAGED AND REUSED. MODIFY MAINTENANCE HOLE FINISH TO MATCH THE FINAL GRADING.
3. PROVIDE NEW DUCT ALONG EXISTING DUCT BANK, UTILIZING EXISTING MAINTENANCE HOLES.
4. EXTEND NEW DUCT LINES FROM (E)TMH-2 TO VMS FACILITIES.
5. EXTEND NEW DUCT LINES AND PROVIDE STUB OUTS FROM (E)TMH-1 TO SSA FACILITIES.

CLIN 0001-0003

- CLIN 0001:**
- SITE PREPARATION WORK FOR VMS FACILITIES.
 - LOONEY STREET AND ELECTRICAL AND TELECOMMUNICATIONS INFRASTRUCTURE IMPROVEMENTS.
 - CONSTRUCTION OF CABLE HUT, RELOCATION OF COMMUNICATIONS HUB FOR CRITICAL OPTICAL FIBER AND COPPER CABLES FROM B4040, AND REESTABLISH THE SERVICES.
 - ENSURE THAT TELECOMMUNICATION SERVICES TO EXISTING ADA BUILDINGS (B4040 THRU B4047) ARE MAINTAINED.
 - RESTORE OPTICAL FIBER CABLES TO K-SITES FROM NEW CABLE HUT.
 - CONSTRUCTION OF VEHICLE MAINTENANCE SHOP, FIRE PUMP HOUSE, WATER STORAGE TANK, AND ASSOCIATED TELECOMMUNICATIONS INFRASTRUCTURE.
- CLIN 0002:**
- CONSTRUCTION OF ORGANIZATIONAL EQUIPMENT STORAGE, POL STORAGE, AND ASSOCIATED TELECOMMUNICATIONS INFRASTRUCTURE.
- CLIN 0003:**
- CONSTRUCTION OF ORGANIZATIONAL VEHICLE PARKING LOT.
 - CONSTRUCTION OF WASH RACK.

US Army Corps of Engineers®

ISSUE DATE:		CONTRACT NO.:		DATE	
DESIGNED BY:	DRAWN BY:	CHECKED BY:	SUBMITTED BY:	SIZE:	FILE NAME:
US ARMY CORPS OF ENGINEERS JAPAN DISTRICT, OKINAWA AREA OFFICE USAED-J UNIT 35132 APO AP 96374-5132		CONTRACT NO.:		AS SHOWN	
SSFM SSFM INTERNATIONAL, INC. 501 SUMNER STREET, SUITE 620 HONOLULU, HAWAII 96817		SCALE:		ISO A1	

KADENA AIR BASE, OKINAWA, JAPAN
VEHICLE MAINTENANCE SHOP
FY20 MCA PN77833

PARTIAL SITE TELECOM PLAN - 1 (CLIN 0001 - CLIN 0003)


SHEET ID

TS202

INTERMEDIATE DESIGN

P
O
N
M
L
K
J
I
H
G
F
E
D
C
B
A

DUCT CABLE SCHEDULE				
TAG	DUCTS	CABLES		REMARKS
(a)	(2) 104mm EXIST	P50-24FF CAO7:301-325+ A.26-50	12SM FOC FR B4040 F.O. LINK B4042	EXIST CABLES TO REMAIN
(b)	(2) 104mm EXIST	P50-24FF CAO7:276-300+ A.26-50	12SM FOC FR B4040 F.O. LINK B4041	EXIST CABLES TO REMAIN
(c)	(2) 104mm EXIST	P50-24FF CAO7:326-350+ A.26-50	12SM FOC FR B4040 F.O. LINK B4043	EXIST CABLES TO REMAIN
(d)	(2) 104mm EXIST	P50-24FF CAO7:351-375+ A.26-50	12SM FOC FR B4040 F.O. LINK B4044	EXIST CABLES TO REMAIN
(e)	(2) 104mm EXIST	P50-24FF CAO7:176-200+ A.26-50	12SM FOC FR B4040 F.O. LINK B4045	EXIST CABLES TO REMAIN
		P50-24FF CAO7:201-225+ A.26-50	12SM FOC FR B4040 F.O. LINK B4047	
		P50-24FF CAO7:226-250+ A.26-50	12SM FOC FR B4040 F.O. LINK B4046	
(f)	(2) 104mm EXIST	P50-24FF CAO7:201-225+ A.26-50	12SM FOC FR B4040 F.O. LINK B4047	EXIST CABLES TO REMAIN
		P50-24FF CAO7:226-250+ A.26-50	12SM FOC FR B4040 F.O. LINK B4046	
(g)	(2) 104mm EXIST	P50-24FF CAO7:226-250+ A.26-50	12SM FOC FR B4040 F.O. LINK B4046	EXIST CABLES TO REMAIN
(h)	(4) 104mm EXIST	P6-24FF CAO7:176-600+ A.1-175	144SM FOC B4040-TMH510 144SM FOC FRROM B718 F.O. LINK B4040, 13-144 (+1-12DD)	EXIST FO CABLES TO BE REPLACED
(i)	(4) 104mm EXIST	P6-24FF CAO9:1-62+ 151-300+ 401-600+ A.301-400+ B.88-100+ C.101-150+ D.63-87 P25-24FF CAJ20:976-1000	48S08F F.O. LINK 10-9:1-48 B926 TO B4065	EXIST CABLES TO REMAIN
	(2) 104mm EXIST		1-12 STRD SM FOC (FO PEDESTAL #1) 1-12 STRD SM FOC (FO PEDESTAL #2)	
(j)	(3) 104mm EXIST	P50-24FF CAO9:501-550	48S08F F.O. LINK 10-9:1-48 B926 TO B4065	EXIST CABLES TO REMAIN
(k)	(2) 104mm EXIST		1-12 STRD SM FOC (FO PEDESTAL #1) 1-12 STRD SM FOC (FO PEDESTAL #2)	EXIST CABLES TO BE REPLACED
(1)	(6) 104mm NEW	1-50PR COPPER (VMS) 1-100PR COPPER (B4040)	144SM FOC B4040-TMH510 144SM FOC FRROM B718 F.O. LINK B4040, 13-144 (+1-12DD) 48SM FOC (B4040) 1-12 STRD SM FOC (FO PEDESTAL #1) 1-12 STRD SM FOC (FO PEDESTAL #2)	RE-TERMINATE 144SM FO TRUNK CABLES AT NEW CABLE HUT PROVIDE NEW FO & COPPER CABLES TO B4040 TO SUPPORT ADA BLDGS PROVIDE NEW FO CABLES FOR FO PEDESTALS AT K-SITES
(2)	(1) 53mm NEW	12-PR COPPER		FIRE PUMP BUILDING
(3)	(3) 104mm NEW	1-50PR COPPER (VMS)	1-12 STRD SM FOC (FO PEDESTAL #1) 1-12 STRD SM FOC (FO PEDESTAL #2) 1-24 STRD SM FO, 1-2 STRD SM FO, CATV (VMS)	PROVIDE NEW FO CABLES FOR FO PEDESTALS AT K-SITES

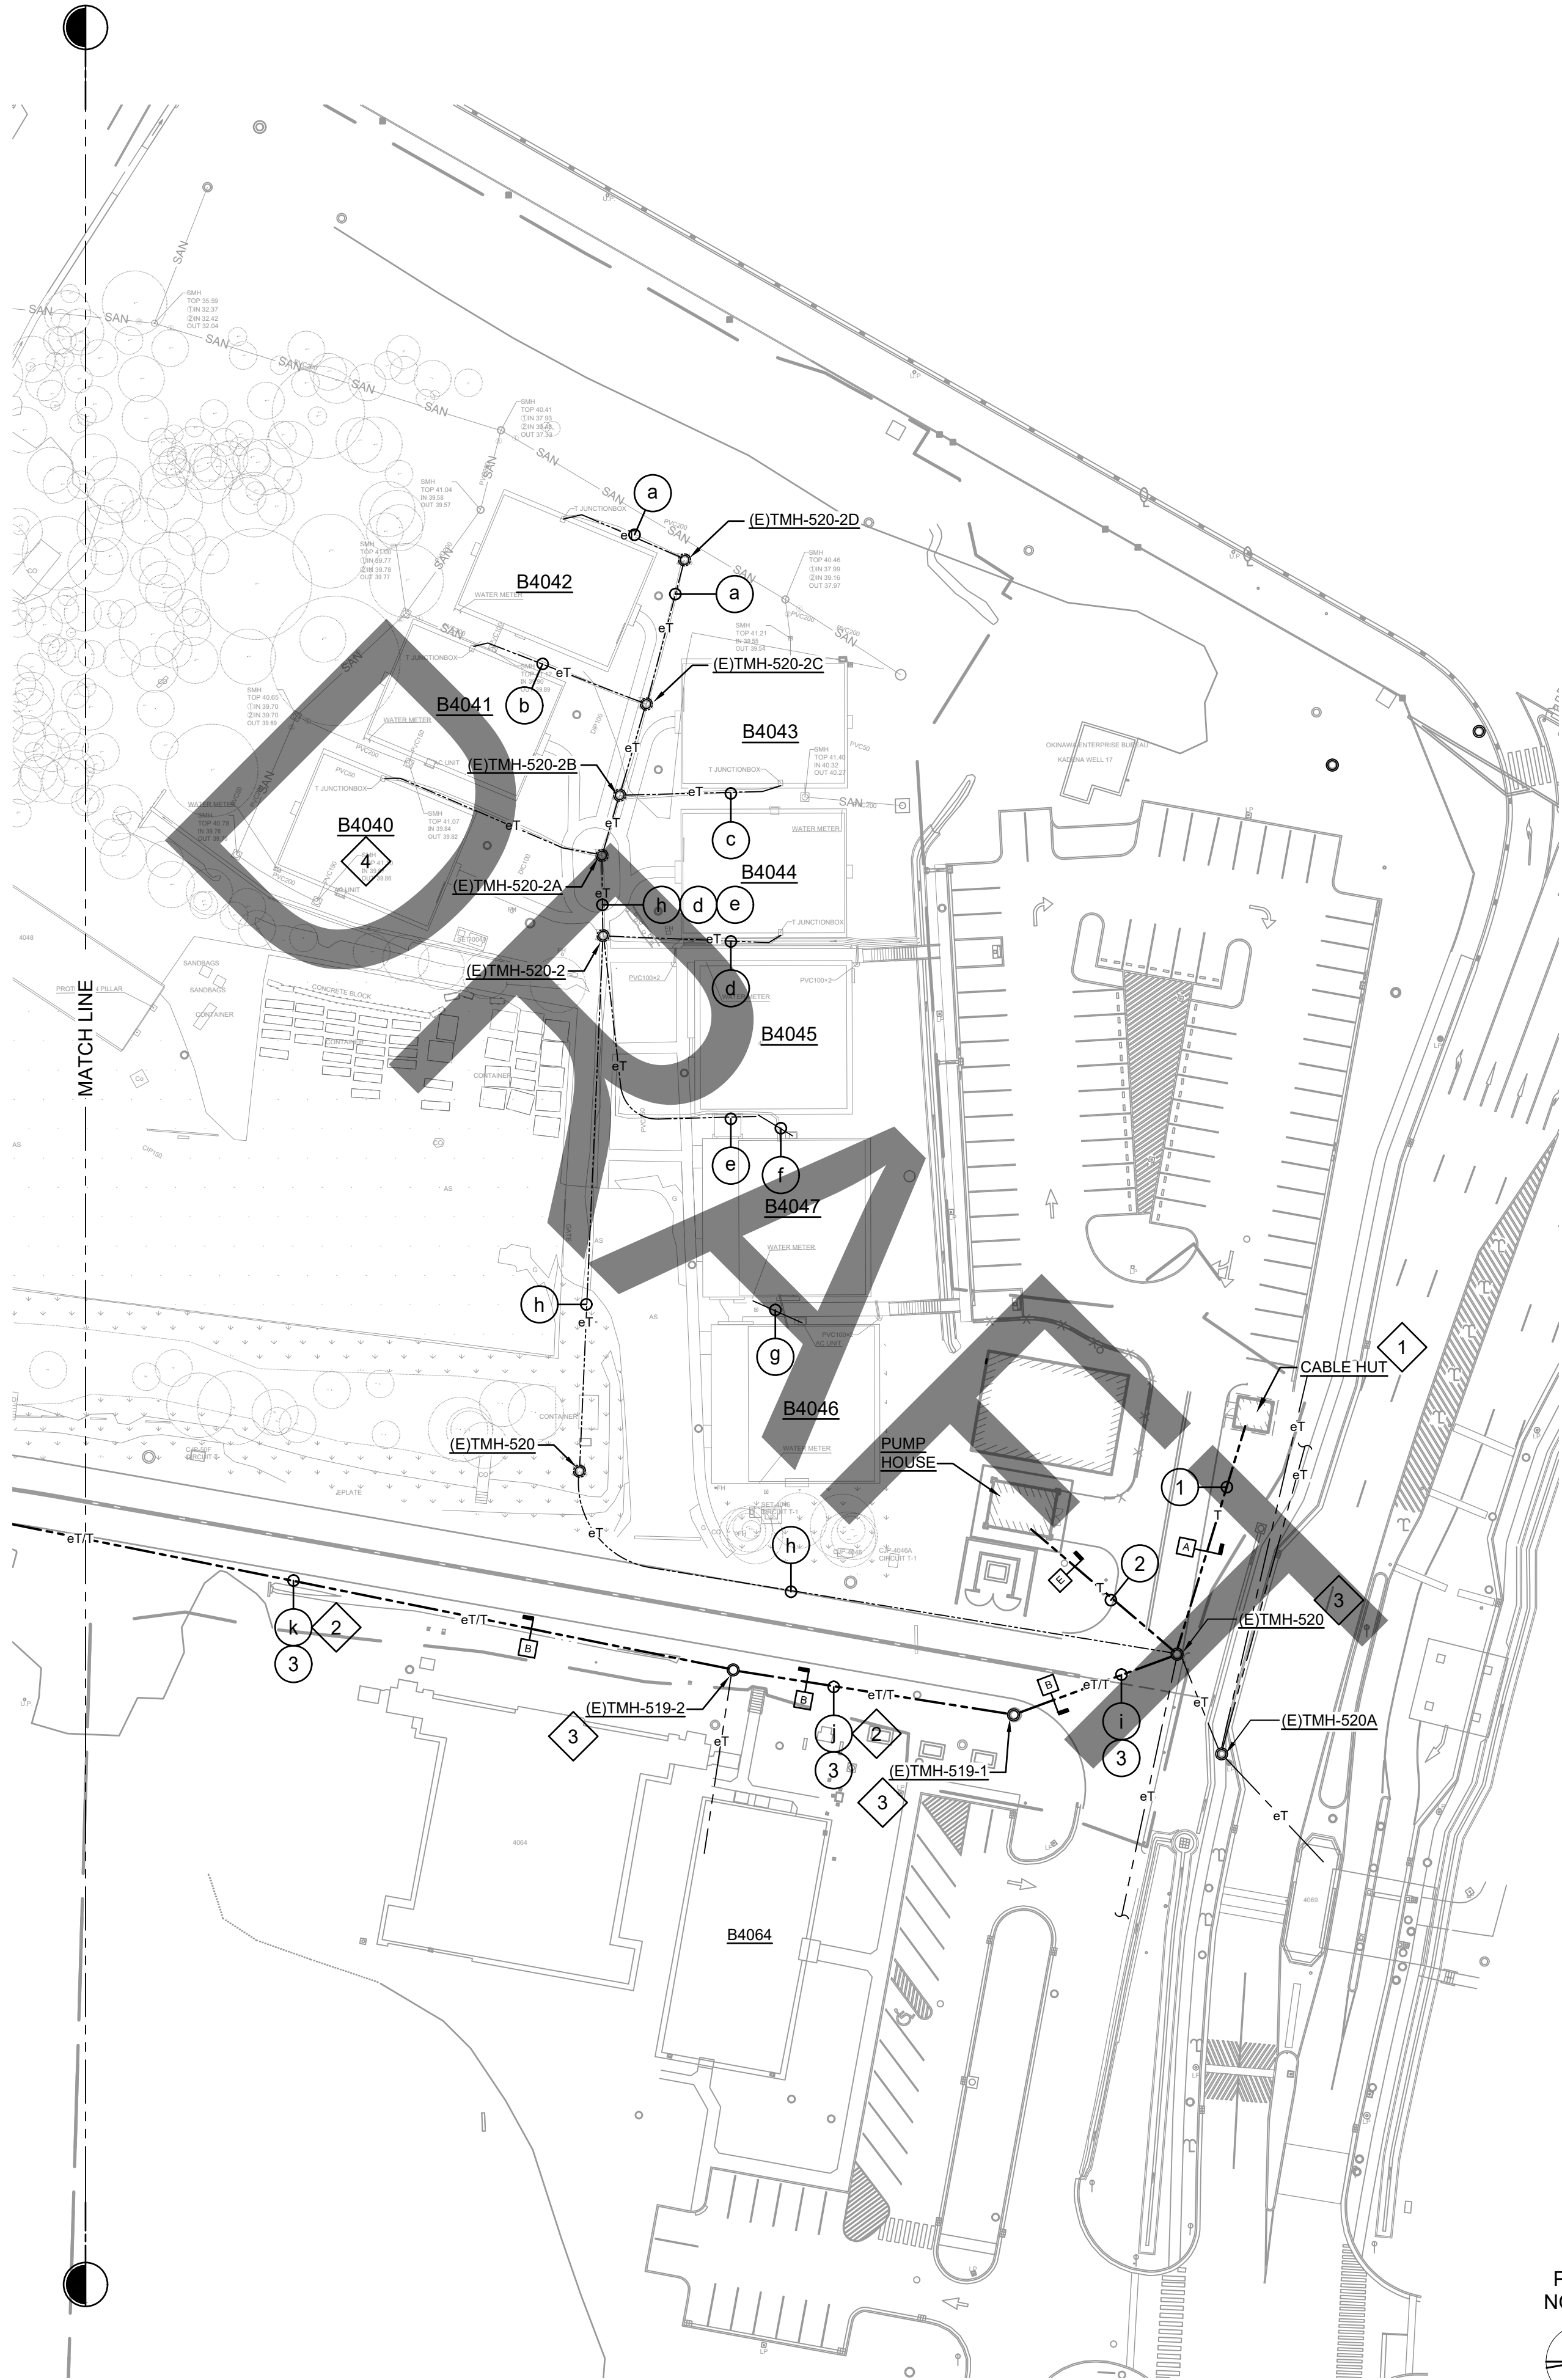

GENERAL NOTES

1. SEE CIVIL AND ELECTRICAL PLANS FOR SITE DEMOLITION WORK AND CLOSELY COORDINATE THE DEMOLITION WORK FOR TELECOMMUNICATIONS SYSTEMS.
2. PRIOR TO ANY TELECOMMUNICATIONS INFRASTRUCTURE AND CABLE DEMOLITION WORK, ENSURE THAT THE NEW INFRASTRUCTURE AND CABLES ARE ESTABLISHED TO MINIMIZE DISRUPTION TO THE OPERATIONS OF THE EXISTING FACILITIES.
3. THE CONTRACTOR SHALL BE RESPONSIBLE TO SUBMIT A PROPOSED PHASING SCHEME IN COORDINATION WITH CIVIL AND ELECTRICAL WORK FOR REVIEW AND APPROVAL PRIOR TO START OF DEMOLITION WORK.

KEY NOTES

1. EXIST FO CABLE HUB LOCATED IN ADA B4040 SHALL BE RELOCATED TO A PROPOSED CABLE HUT AND ALL EXIST CRITICAL SERVICES SHALL BE RE-ESTABLISHED PRIOR TO DEMOLITION OF COMMUNICATION CABLES AND INFRASTRUCTURE.
2. EXIST OPTICAL FIBER CABLES SERVING THE K-SITES SHALL BE REMOVED AND RESTORED BACK TO THE NEW CABLE HUT UTILIZING EXIST AND NEW INFRASTRUCTURE.
3. EXISTING MAINTENANCE HOLES AND DUCTS SHALL BE SALVAGED AND REUSED. MODIFY MAINTENANCE HOLE FINISH TO MATCH THE FINAL GRADING.
4. EXISTING TELECOMMUNICATION SERVICES TO ADA BUILDINGS (B4040 THRU B4047) SHALL REMAIN IN SERVICE BY RECONNECTING THE SERVER IN B4040 TO NEW CABLE HUT.

CLIN 0001-0003

- CLIN 0001:
- SITE PREPARATION WORK FOR VMS FACILITIES.
 - LOONEY STREET AND ELECTRICAL AND TELECOMMUNICATIONS INFRASTRUCTURE IMPROVEMENTS.
 - CONSTRUCTION OF CABLE HUT, RELOCATION OF COMMUNICATIONS HUB FOR CRITICAL OPTICAL FIBER AND COPPER CABLES FROM B4040, AND REESTABLISH THE SERVICES.
 - ENSURE THAT TELECOMMUNICATION SERVICES TO EXISTING ADA BUILDINGS (B4040 THRU B4047) ARE MAINTAINED.
 - RESTORE OPTICAL FIBER CABLES TO K-SITES FROM NEW CABLE HUT.
 - CONSTRUCTION OF VEHICLE MAINTENANCE SHOP, FIRE PUMP HOUSE, WATER STORAGE TANK, AND ASSOCIATED TELECOMMUNICATIONS INFRASTRUCTURE.
- CLIN 0002:
- CONSTRUCTION OF ORGANIZATIONAL EQUIPMENT STORAGE, POL STORAGE, AND ASSOCIATED TELECOMMUNICATIONS INFRASTRUCTURE.
- CLIN 0003:
- CONSTRUCTION OF ORGANIZATIONAL VEHICLE PARKING LOT.
 - CONSTRUCTION OF WASH RACK.

US Army Corps of Engineers®

ISSUE DATE:	DESIGNED BY:	US ARMY CORPS OF ENGINEERS
SOLICITATION NO.:	DRAWN BY:	JAPAN DISTRICT, OKINAWA AREA OFFICE
CONTRACT NO.:	CHECKED BY:	USAED-J UNIT 35132
SCALE:	SUBMITTED BY:	APD 96374-5132
AS SHOWN	FILE NAME:	SSFM
	SIZE:	SSFM INTERNATIONAL, INC.
	ISO A1	501 SUMNER STREET, SUITE 620
		HONOLULU, HAWAII 96817

PARTIAL SITE TELECOM PLAN - 2 (CLIN 0001 - CLIN 0003)

KADENA AIR BASE, OKINAWA, JAPAN
VEHICLE MAINTENANCE SHOP
FY20 MCA PN77833


SHEET ID

TS203

INTERMEDIATE DESIGN

SITE K

P
O
N
M
L
K
J
I
H
G
F
E
D
C
B
A

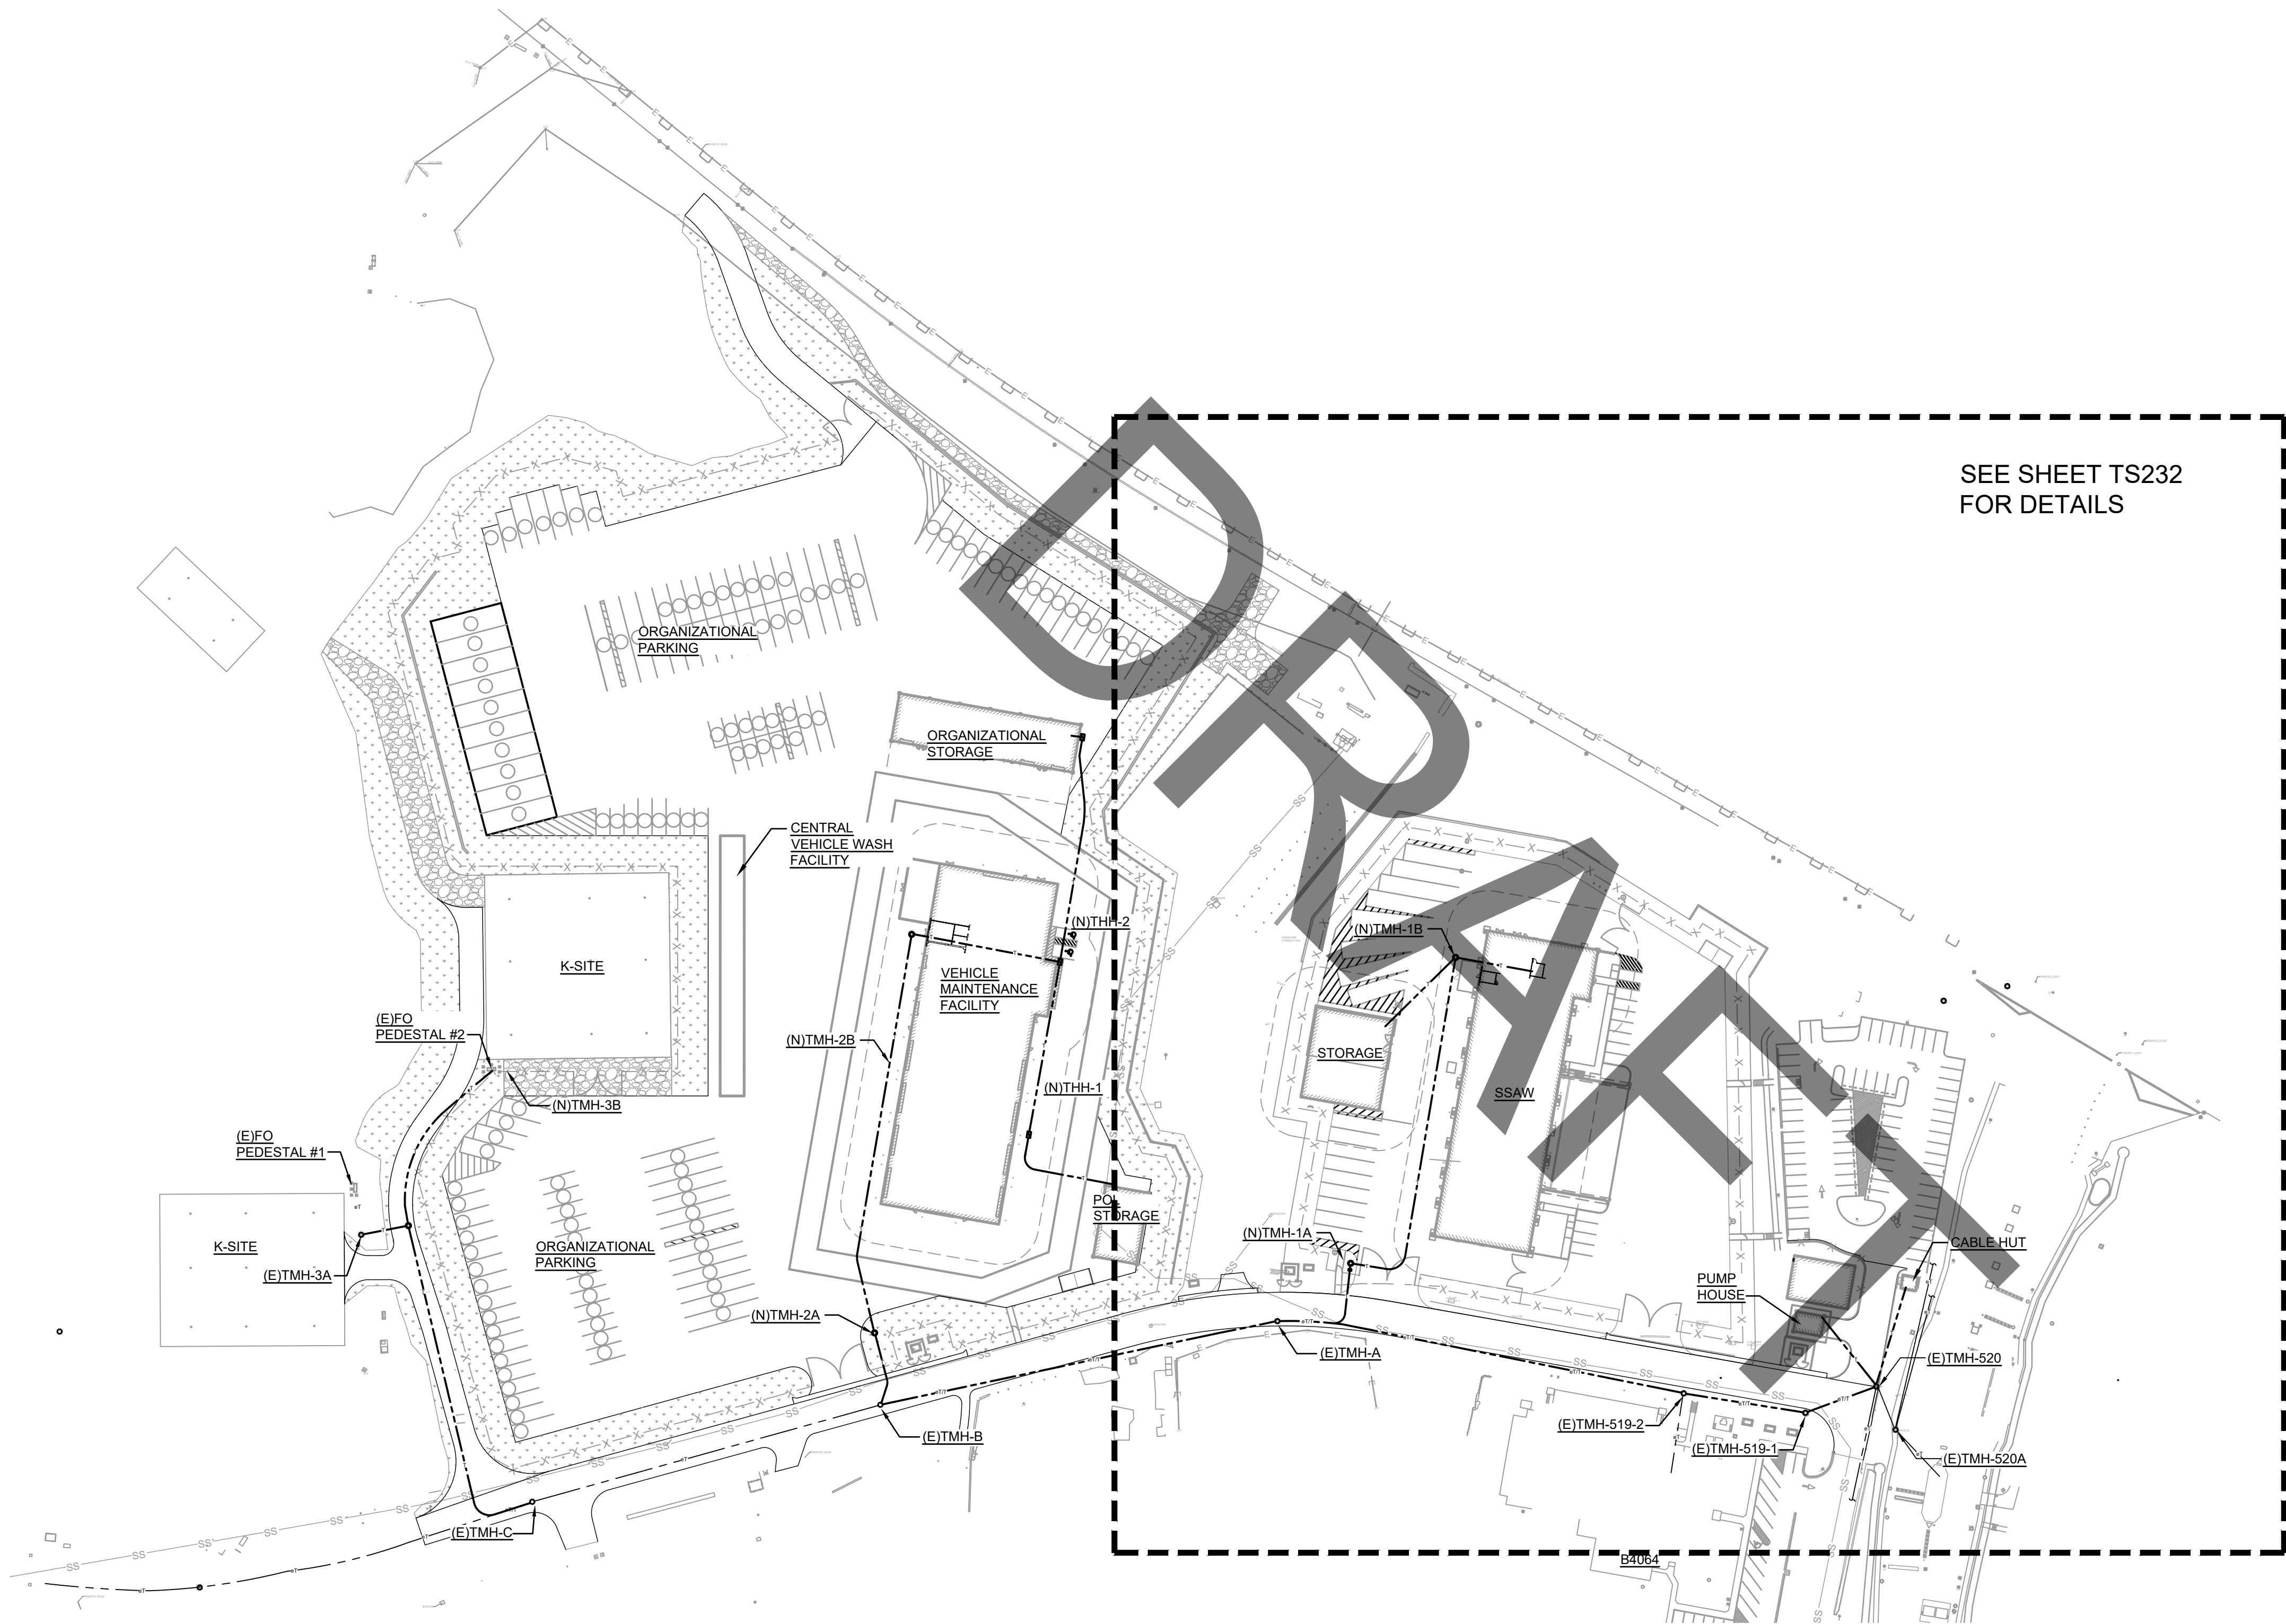

A1 OVERALL SITE TELECOMMUNICATION PLAN (CLIN0004)
1:1000

GENERAL NOTES

1. SEE CIVIL AND ELECTRICAL PLANS FOR SITE DEMOLITION WORK AND CLOSELY COORDINATE THE DEMOLITION WORK FOR TELECOMMUNICATIONS SYSTEMS.
2. PRIOR TO ANY TELECOMMUNICATIONS INFRASTRUCTURE AND CABLE DEMOLITION WORK, ENSURE THAT THE NEW INFRASTRUCTURE AND CABLES ARE ESTABLISHED TO MINIMIZE DISRUPTION TO THE OPERATIONS OF THE EXISTING FACILITIES.
3. THE CONTRACTOR SHALL BE RESPONSIBLE TO SUBMIT A PROPOSED PHASING SCHEME IN COORDINATION WITH CIVIL AND ELECTRICAL WORK FOR REVIEW AND APPROVAL PRIOR TO START OF DEMOLITION WORK.

KEY NOTES

CLIN 0004

- CLIN 0004**
- CONSTRUCTINO OF TEMPORARY FACILITIES AT SWING SPACE SITE MUST BE COMPLETED PRIOR TO DEMOLITION OF EXISTING ADA BUILDINGS (B4040 THRU B4047) AND SITE PREPARATION WORK FOR SSA FACILITIES.
 - CONSTRUCTION OF NEW SUPPLY SUPPORT ACTIVITY (SSA) WAREHOUSE, STORAGE SHED AND ASSOCIATED TELECOMMUNICATIONS INFRASTRUCTURE.
 - CONSTRUCTION OF SSA PARKING LOT.

US Army Corps
of Engineers®

ISSUE DATE:		MARK		DATE
DESIGNED BY:	DRAWN BY:	CHECKED BY:	SUBMITTED BY:	FILE NAME:
JAPAN DISTRICT, OKINAWA AREA OFFICE	USAED-J UNIT 35132	APD, AP 96374-5132	SSFM INTERNATIONAL, INC.	501 SUMNER STREET, SUITE 620 HONOLULU, HAWAII 96817
SOLICITATION NO.:		CONTRACT NO.:		SCALE:
				AS SHOWN
SIZE:		ISO A1		

KADENA AIR BASE, OKINAWA, JAPAN
VEHICLE MAINTENANCE SHOP
FY20 MCA PN77833


OVERALL SITE TELECOM PLAN (CLIN 0004)

SHEET ID

TS231

INTERMEDIATE DESIGN

P
O
N
M
L
K
J
I
H
G
F
E
D
C
B
A

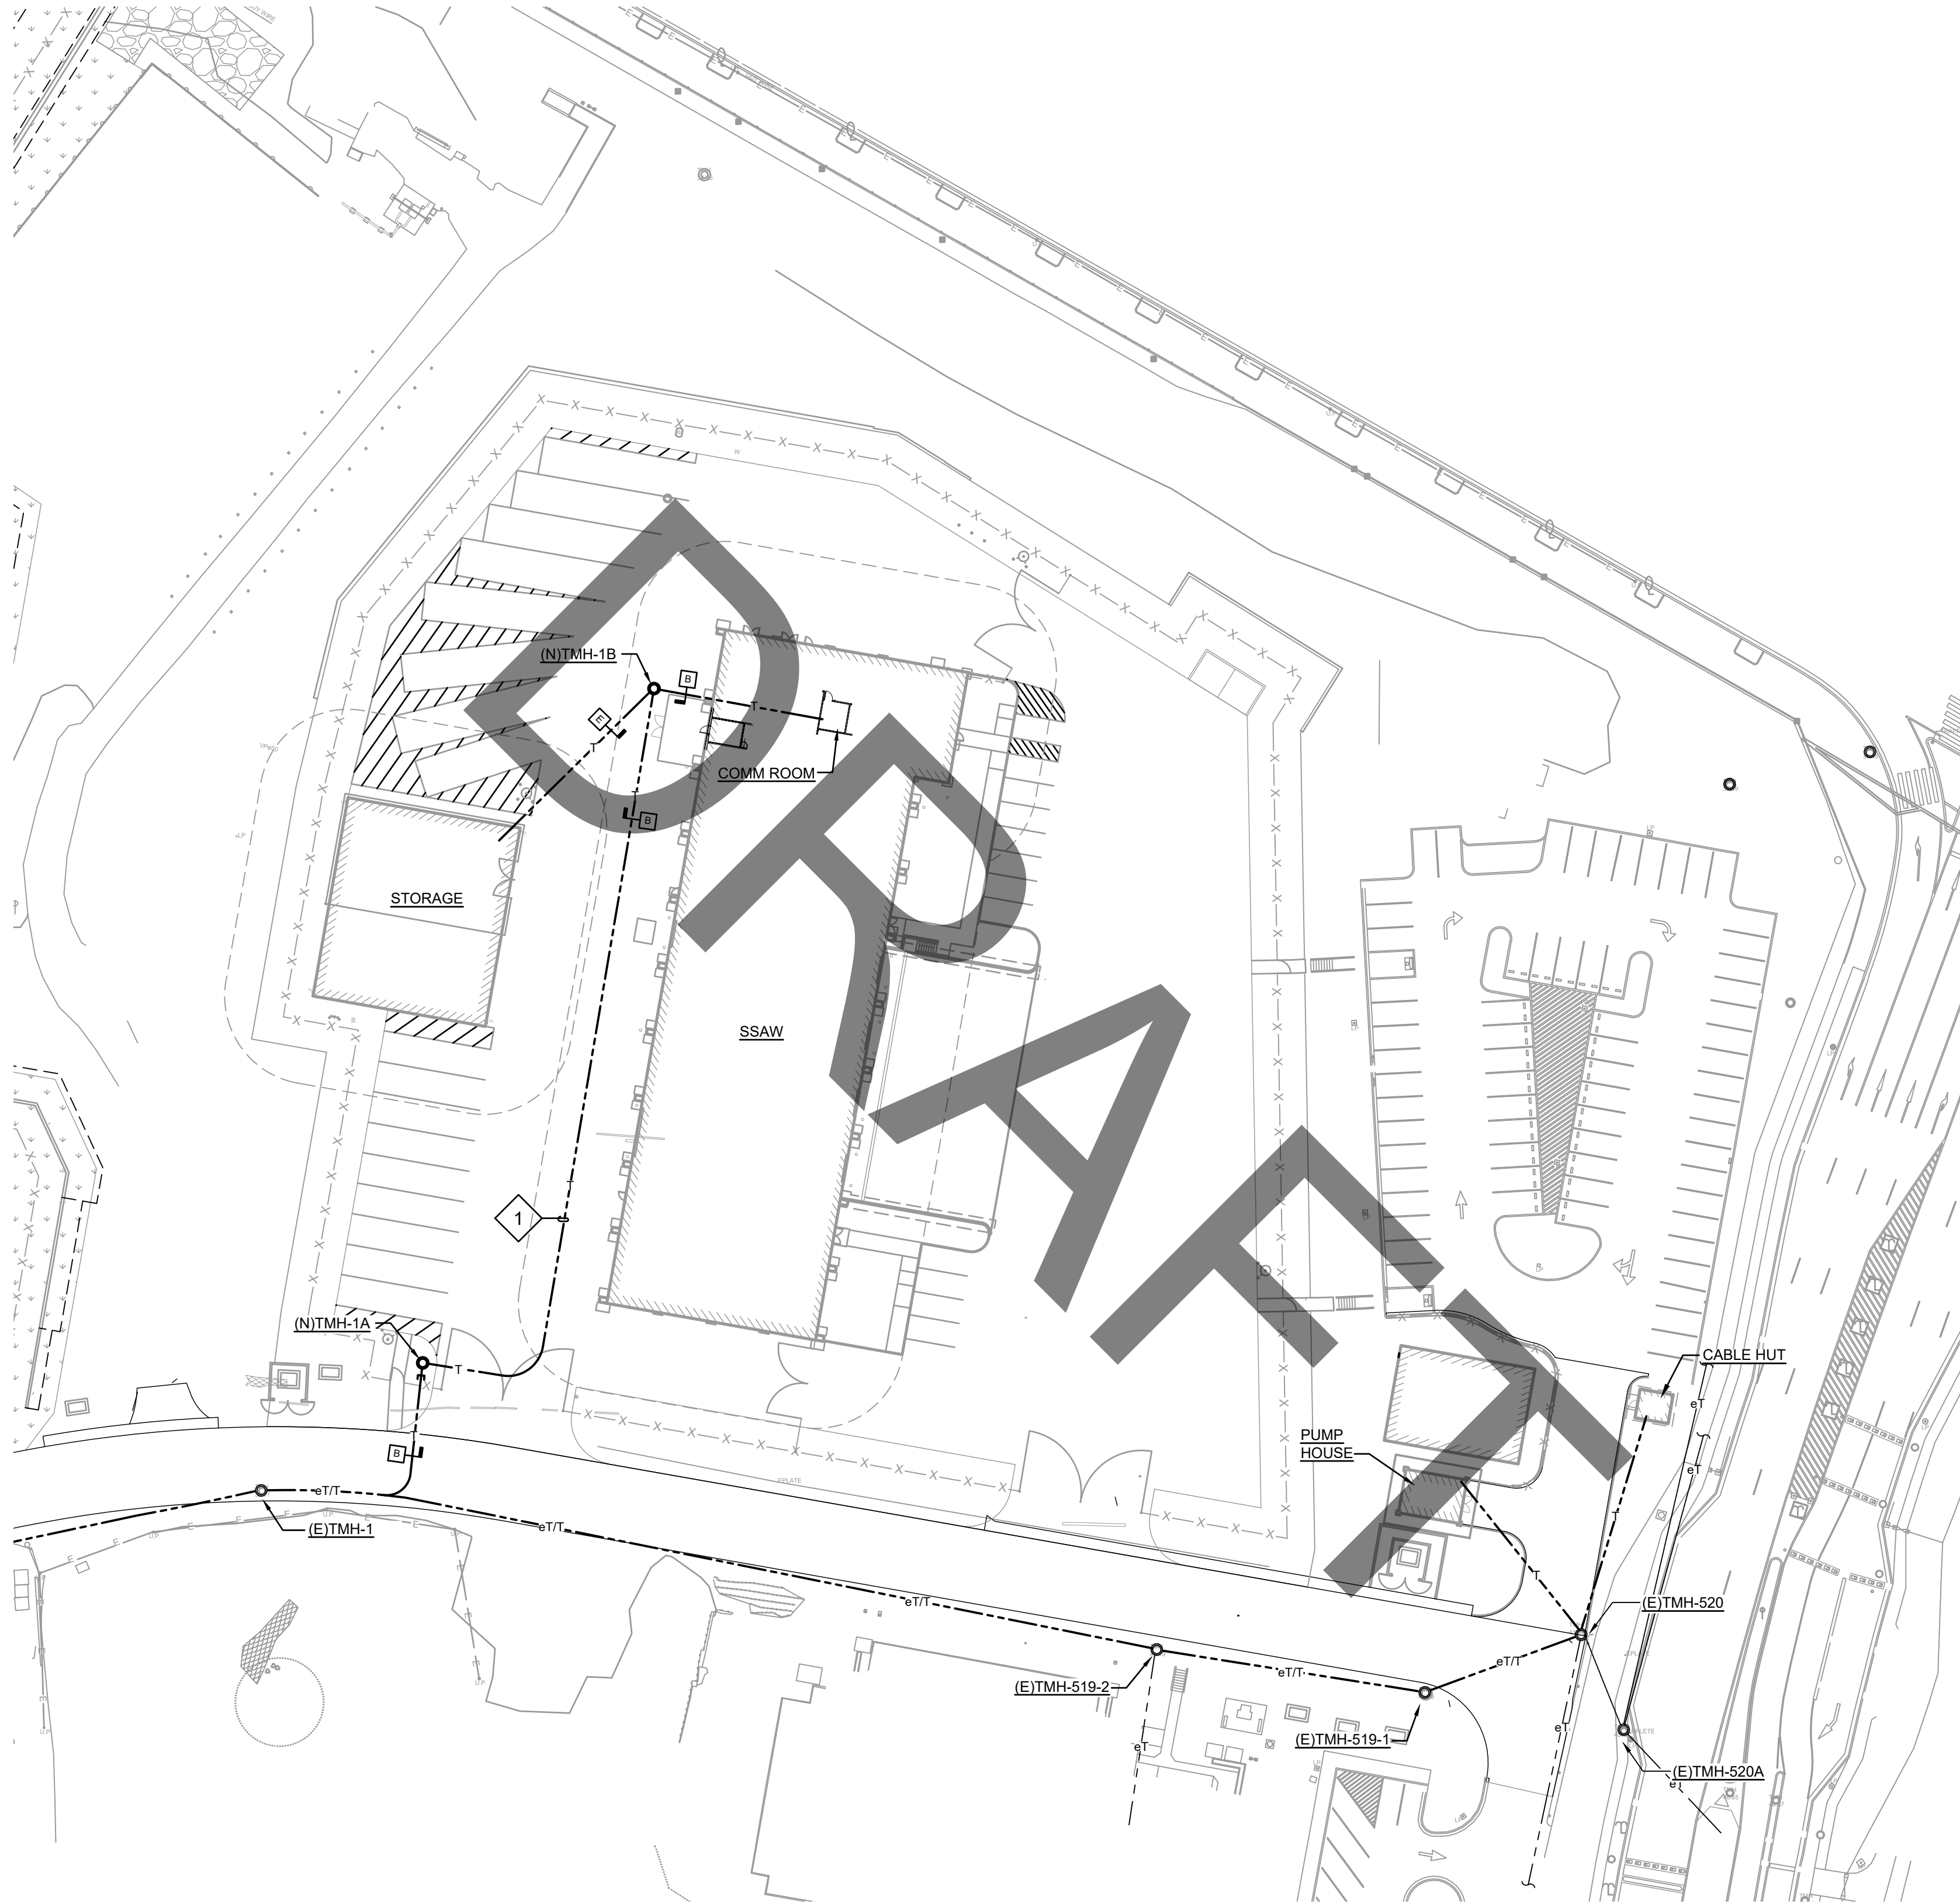

A1 PARTIAL SITE TELECOMMUNICATION PLAN (CLIN0004)
1:500

GENERAL NOTES

1. SEE CIVIL AND ELECTRICAL PLANS FOR SITE DEMOLITION WORK AND CLOSELY COORDINATE THE DEMOLITION WORK FOR TELECOMMUNICATIONS SYSTEMS.
2. PRIOR TO ANY TELECOMMUNICATIONS INFRASTRUCTURE AND CABLE DEMOLITION WORK, ENSURE THAT THE NEW INFRASTRUCTURE AND CABLES ARE ESTABLISHED TO MINIMIZE DISRUPTION TO THE OPERATIONS OF THE EXISTING FACILITIES.
3. THE CONTRACTOR SHALL BE RESPONSIBLE TO SUBMIT A PROPOSED PHASING SCHEME IN COORDINATION WITH CIVIL AND ELECTRICAL WORK FOR REVIEW AND APPROVAL PRIOR TO START OF DEMOLITION WORK.

KEY NOTES

- 1** EXTEND NEW DUCT LINES FROM (E)TMH-1 TO SSAW FACILITIES.



US Army Corps
of Engineers®

MARK	DESCRIPTION	DATE

DESIGNED BY:	ISSUE DATE:
DRAWN BY:	SOLICITATION NO.:
CHECKED BY:	CONTRACT NO.:
SUBMITTED BY:	SCALE:
SIZE:	FILE NAME:
ISO A1	AS SHOWN
US ARMY CORPS OF ENGINEERS JAPAN DISTRICT, OKINAWA AREA OFFICE USAED-J, UNIT 35132 APO, AP 96374-5132 SSFM SSFM INTERNATIONAL, INC. 501 SUMNER STREET, SUITE 620 HONOLULU, HAWAII 96817	

CLIN 0004




- CLIN 0004**
- CONSTRUCTINO OF TEMPORARY FACILITIES AT SWING SPACE SITE MUST BE COMPLETED PRIOR TO DEMOLITION OF EXISTING ADA BUILDINGS (B4040 THRU B4047) AND SITE PREPARATION WORK FOR SSA FACILITIES.
 - CONSTRUCTION OF NEW SUPPLY SUPPORT ACTIVITY (SSA) WAREHOUSE, STORAGE SHED AND ASSOCIATED TELECOMMUNICATIONS INFRASTRUCTURE.
 - CONSTRUCTION OF SSA PARKING LOT.

KADENA AIR BASE, OKINAWA, JAPAN VEHICLE MAINTENANCE SHOP FY20 MCA PN77833	PARTIAL SITE TELECOM PLAN (CLIN 0004)
---	---------------------------------------

SHEET ID
TS232

INTERMEDIATE DESIGN

P
O
N
M
L
K
J
I
H
G
F
E
D
C
B
A

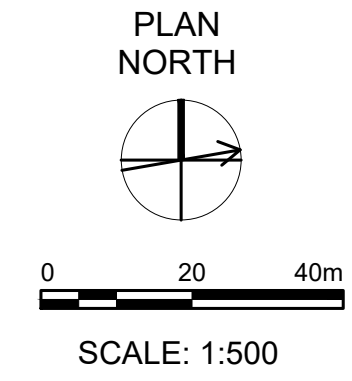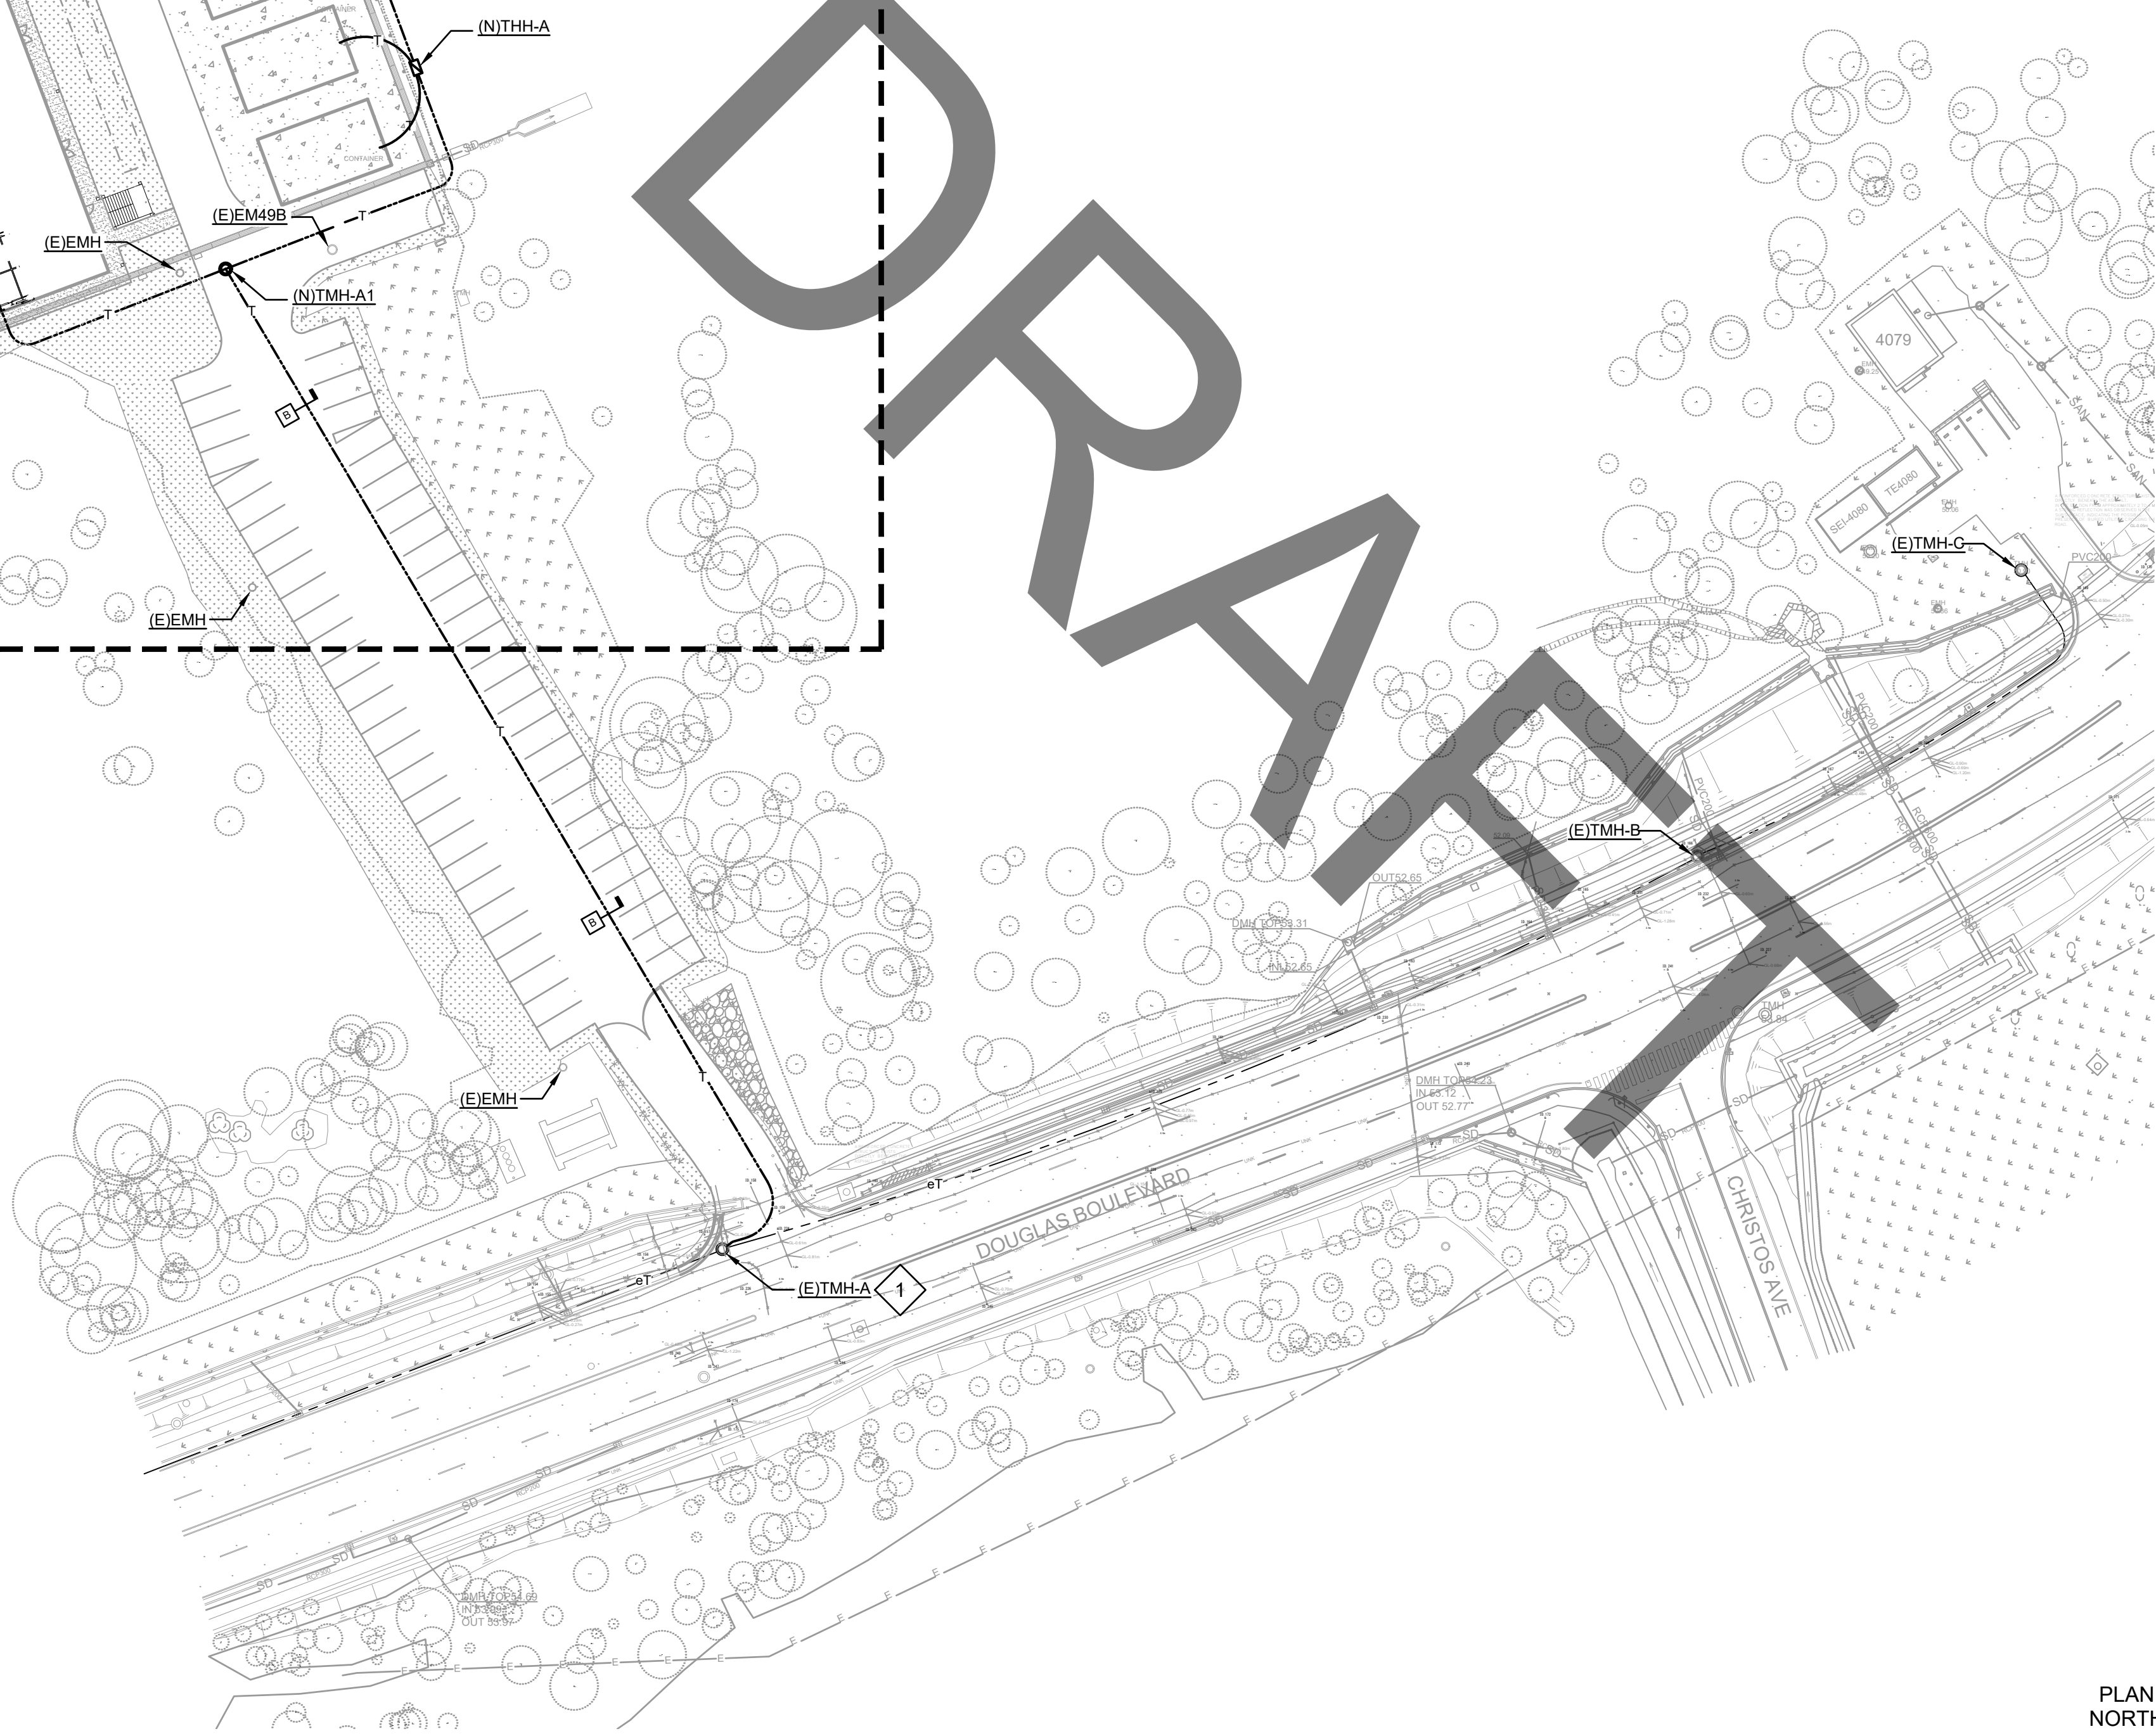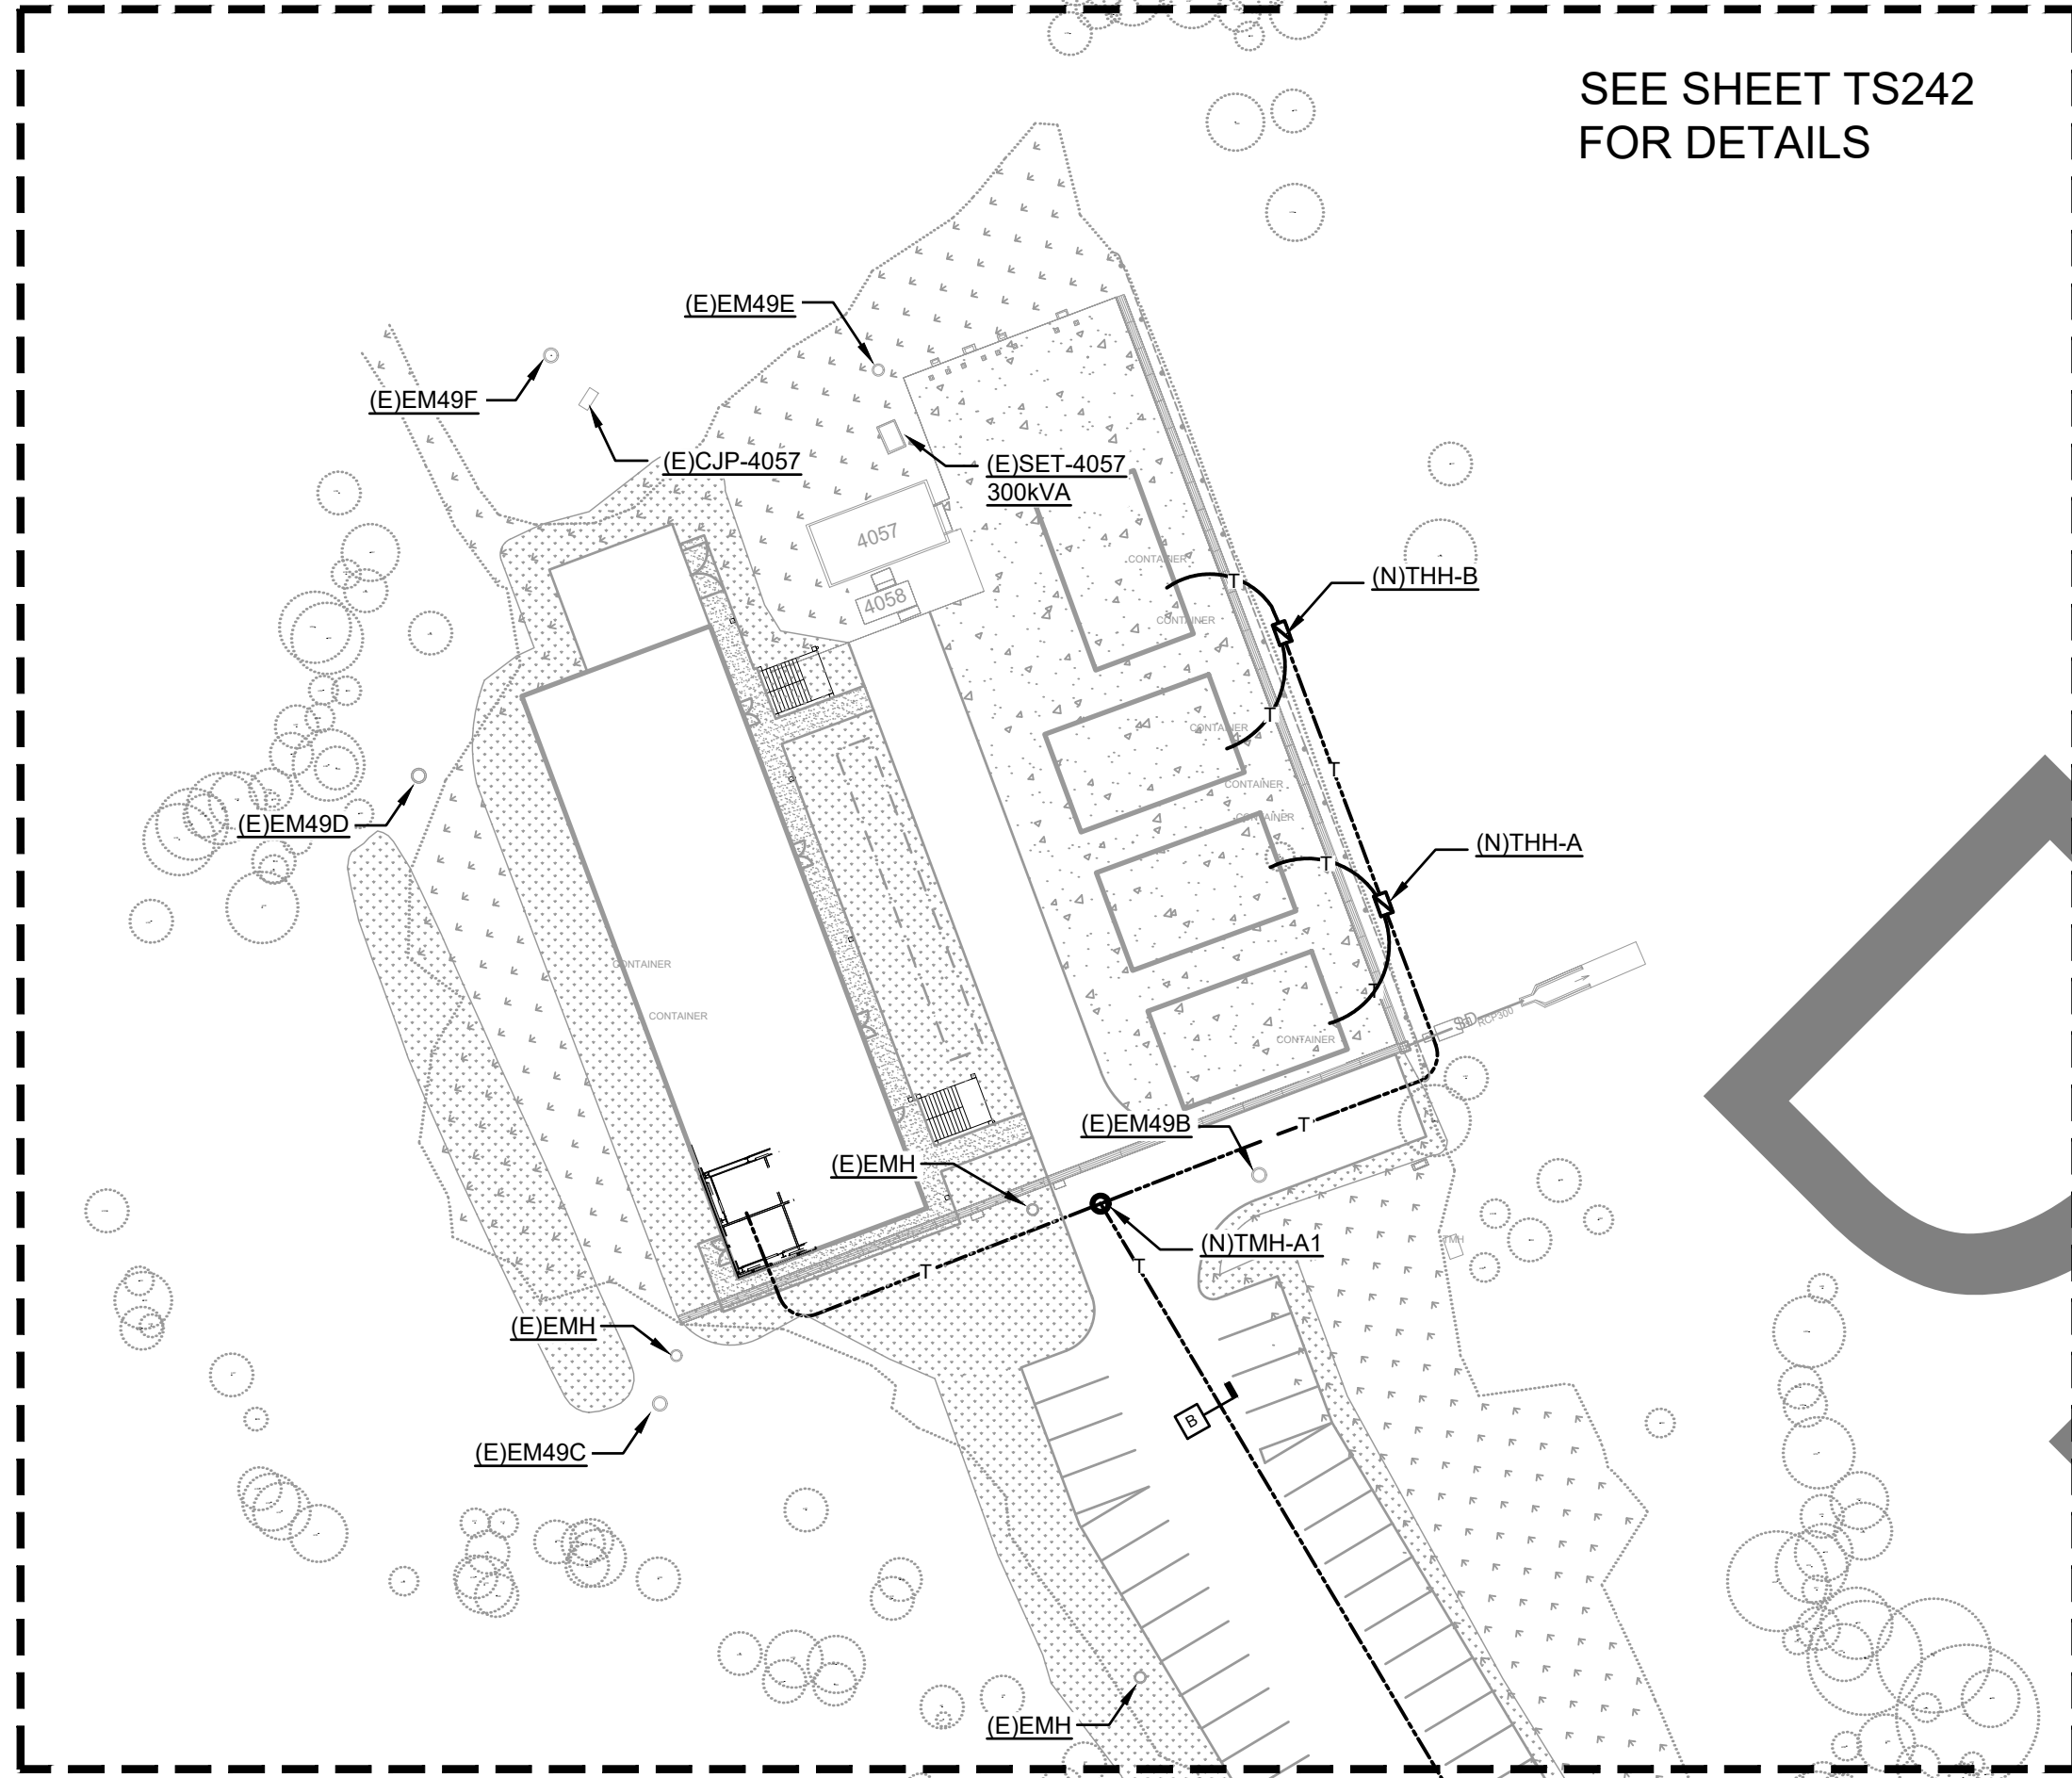

A1 OVERALL SITE TELECOMMUNICATIONS PLAN - SWING SPACE (CLIN0004)

GENERAL NOTES

1. SEE CIVIL AND ELECTRICAL PLANS FOR SITE DEMOLITION WORK AND CLOSELY COORDINATE THE DEMOLITION WORK FOR TELECOMMUNICATIONS SYSTEMS.
2. PRIOR TO ANY TELECOMMUNICATIONS INFRASTRUCTURE AND CABLE DEMOLITION WORK, ENSURE THAT THE NEW INFRASTRUCTURE AND CABLES ARE ESTABLISHED TO MINIMIZE DISRUPTION TO THE OPERATIONS OF THE EXISTING FACILITIES.
3. THE CONTRACTOR SHALL BE RESPONSIBLE TO SUBMIT A PROPOSED PHASING SCHEME IN COORDINATION WITH CIVIL AND ELECTRICAL WORK FOR REVIEW AND APPROVAL PRIOR TO START OF DEMOLITION WORK.

KEY NOTES

- 1** MODIFY EXISTING MAINTENANCE HOLE FINISH TO MATCH THE FINAL GRADING.

CLIN 0004

- CLIN 0004**
- CONSTRUCTINO OF TEMPORARY FACILITIES AT SWING SPACE SITE MUST BE COMPLETED PRIOR TO DEMOLITION OF EXISTING ADA BUILDINGS (B4040 THRU B4047) AND SITE PREPARATION WORK FOR SSA FACILITIES.
 - CONSTRUCTION OF NEW SUPPLY SUPPORT ACTIVITY (SSA) WAREHOUSE, STORAGE SHED AND ASSOCIATED TELECOMMUNICATIONS INFRASTRUCTURE.
 - CONSTRUCTION OF SSA PARKING LOT.

US Army Corps of Engineers®

ISSUE DATE:		SOLICITATION NO.:		CONTRACT NO.:		SCALE:		AS SHOWN		FILE NAME:		ISO A1	
DESIGNED BY:		DRAWN BY:		CHECKED BY:		SUBMITTED BY:		SIZE:		FILE NAME:		ISO A1	

US ARMY CORPS OF ENGINEERS
JAPAN DISTRICT, OKINAWA AREA OFFICE
USAED-J UNIT 35132
APO, AP 96374-5132

SSFM
SSFM INTERNATIONAL, INC.
501 SUMNER STREET, SUITE 620
HONOLULU, HAWAII 96817


KADENA AIR BASE, OKINAWA, JAPAN
VEHICLE MAINTENANCE SHOP
FY20 MCA PN77833

OVERALL SITE TELECOM PLAN - COF SS (CLIN 0004)

SHEET ID

TS241

INTERMEDIATE DESIGN

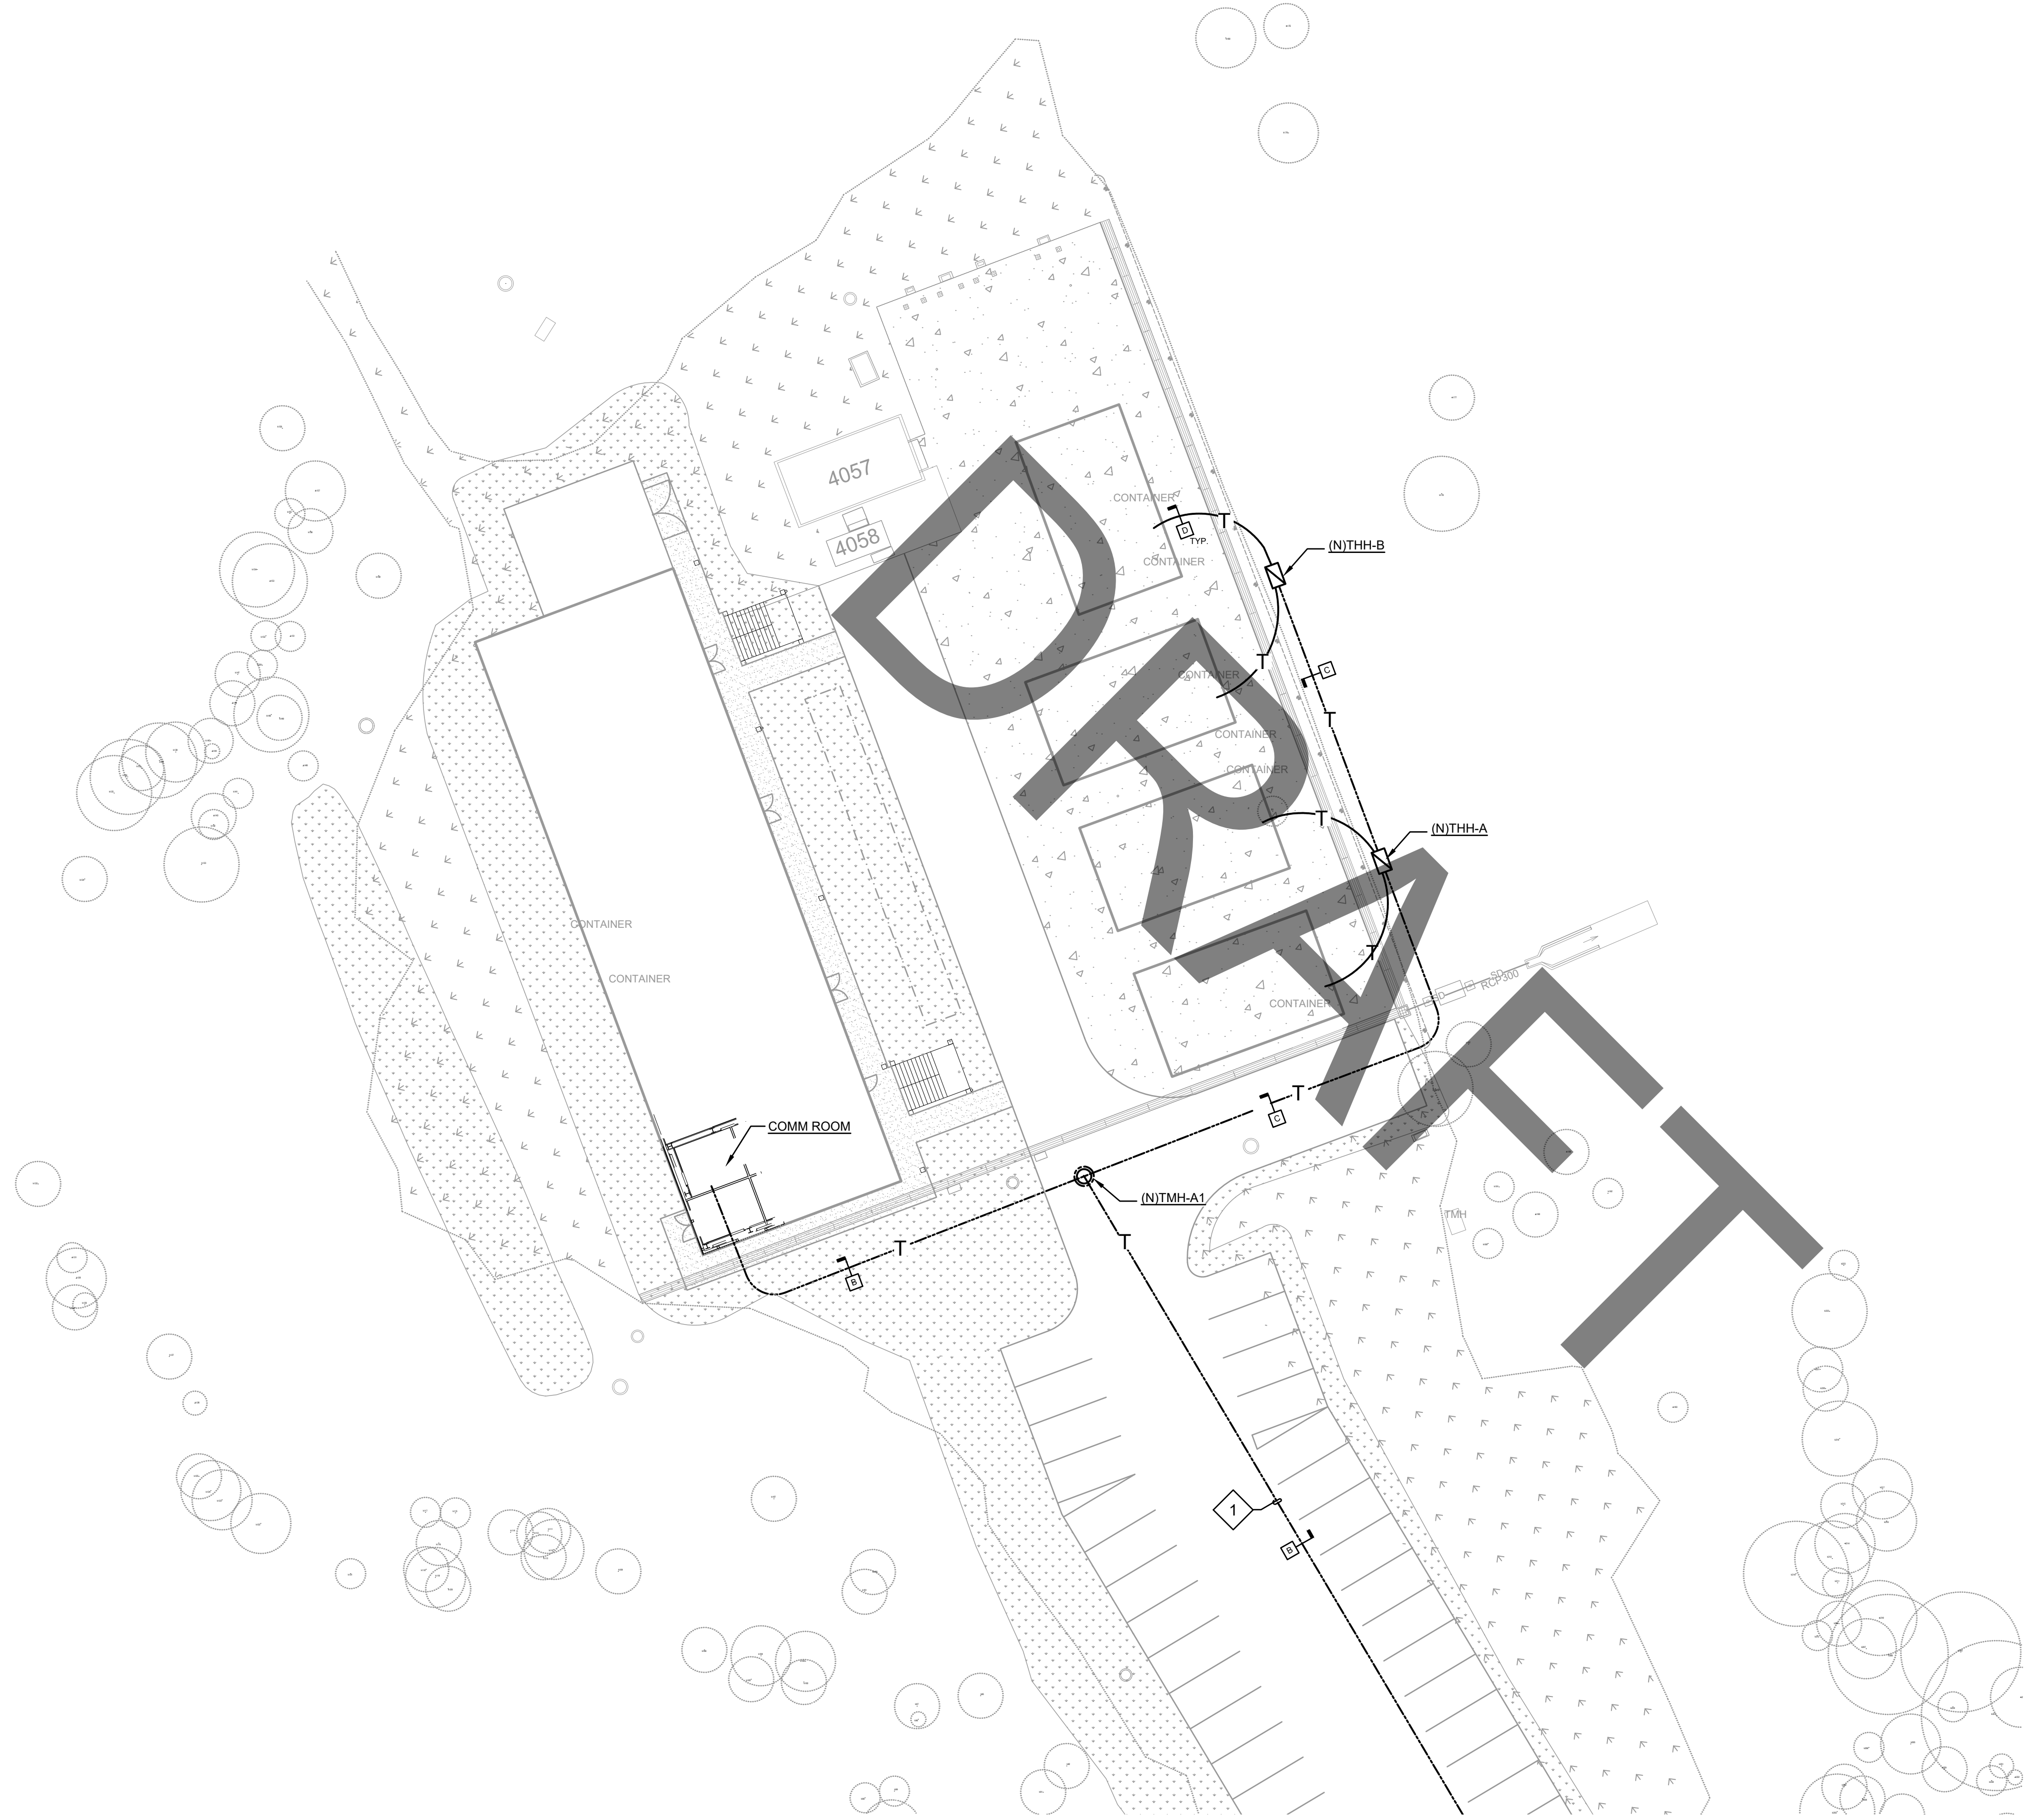

A1 PARTIAL SITE TELECOMMUNICATIONS PLAN - SWING SPACE (CLIN0004)

GENERAL NOTES

1. SEE CIVIL AND ELECTRICAL PLANS FOR SITE DEMOLITION WORK AND CLOSELY COORDINATE THE DEMOLITION WORK FOR TELECOMMUNICATIONS SYSTEMS.
2. PRIOR TO ANY TELECOMMUNICATIONS INFRASTRUCTURE AND CABLE DEMOLITION WORK, ENSURE THAT THE NEW INFRASTRUCTURE AND CABLES ARE ESTABLISHED TO MINIMIZE DISRUPTION TO THE OPERATIONS OF THE EXISTING FACILITIES.
3. THE CONTRACTOR SHALL BE RESPONSIBLE TO SUBMIT A PROPOSED PHASING SCHEME IN COORDINATION WITH CIVIL AND ELECTRICAL WORK FOR REVIEW AND APPROVAL PRIOR TO START OF DEMOLITION WORK.

KEY NOTES

- 1 EXTEND NEW DUCT LINES FROM (E)TMH-A TO COA AND ARMORY FACILITIES.



**U.S. Army Corps
Engineers®**

[illegible]

US ARMY CORP OF ENGINEERS JAPAN DISTRICT OFFICE 501 SUMNER STREET, SUITE 620 HONOLULU, HAWAII 96813 APO AP 96374-5132		SSFWM INTERNATIONAL, INC 501 SUMNER STREET, SUITE 620 HONOLULU, HAWAII 96813	
DRAWN BY:	SOLICITATION NO.:	CHECKED BY:	CONTRACT NO.:
		SUBMITTED BY:	SCALE:
SIZE:	FILE NAME:	AS SHOWN	
ISO A1			


KADENA AIR BASE, OKINAWA, JAPAN
VEHICLE MAINTENANCE SHOP
FY20 MCA PN77833

SHEET ID

S242

INTERMEDIATE DESIGN

P —
 O —
 N —
 M —
 L —
 K —
 J —
 I —
 H —
 G —
 F —
 E —
 D —
 C —
 B —
 A

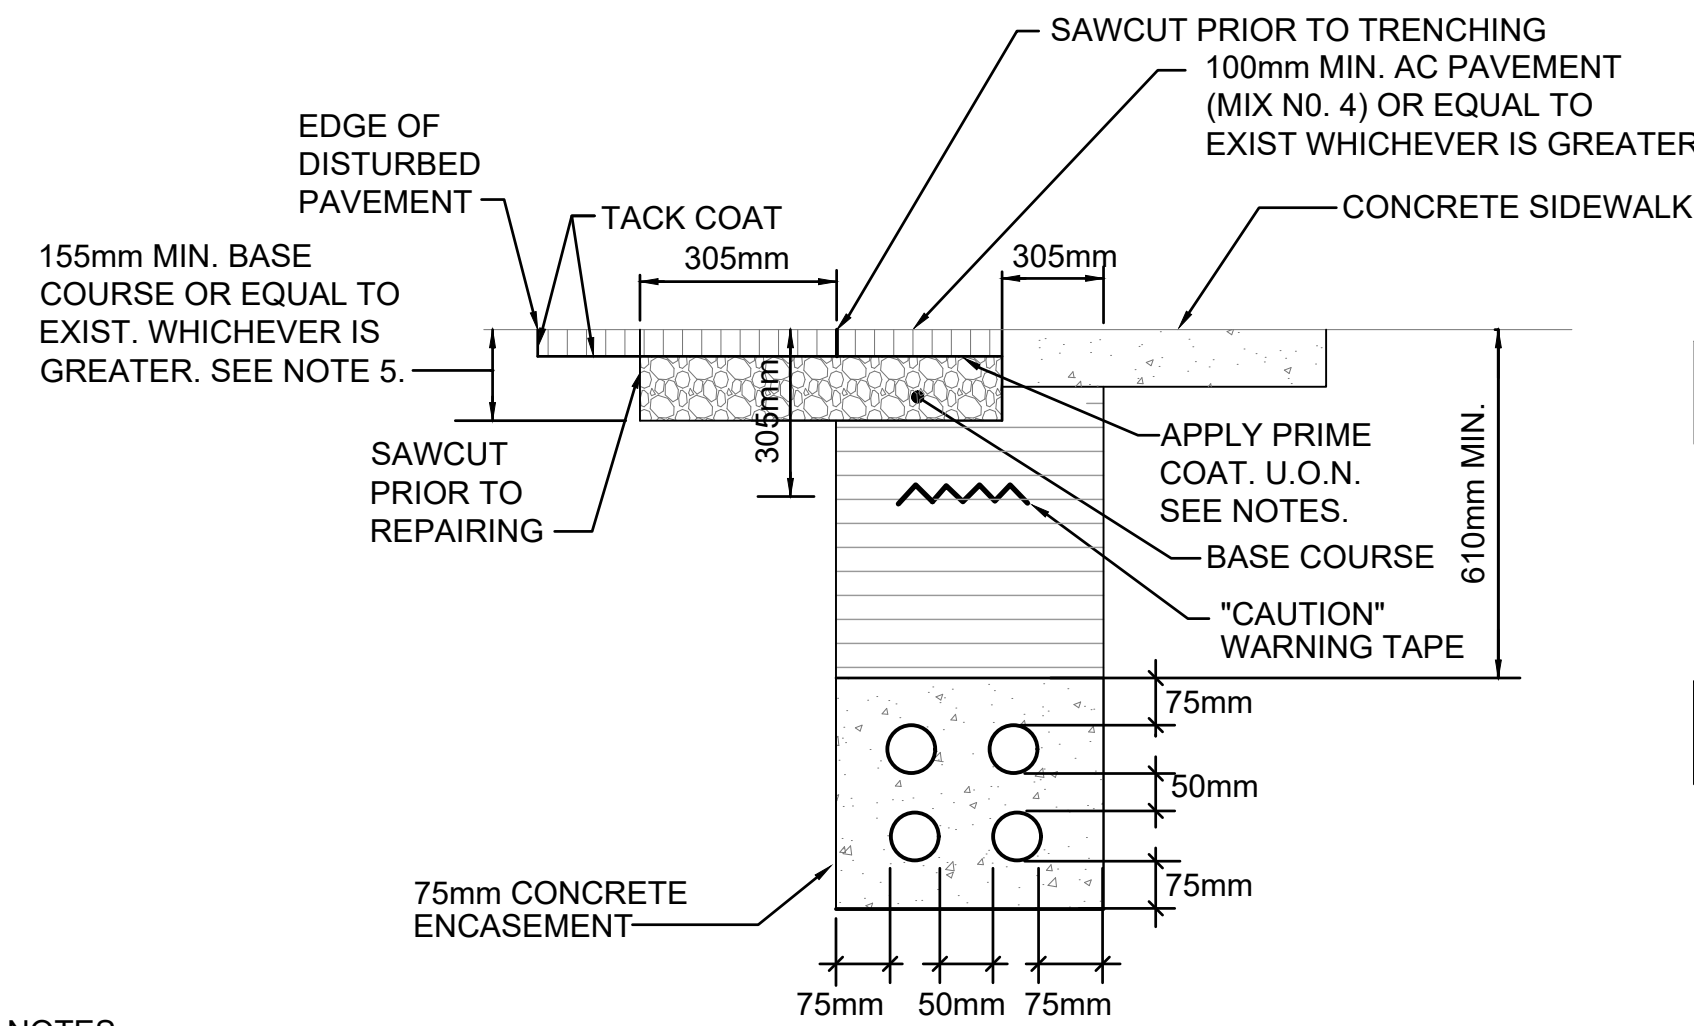

BACKFILL NOTES:

TYPE "A" BACKFILL - EARTH & GRAVEL.
ROCK SIZE TO BE 25mm MAX & THE
MIXTURE TO CONTAIN NOT MORE
THAN 50% BY VOLUME OF ROCK
PARTICLES. 95% COMPACTION.



CONCRETE - 75mm ENCASEMENT,
2500 PSI COMPRESSIVE STRENGTH
@ 28 DAYS.







NOTES:

1. CONCRETE ENCASED CONDUITS SHALL BE PVC SCHEDULE 40.
2. PROVIDE ALL EMPTY CONDUITS WITH PULLWIRE. PROVIDE ALL EMPTY COMMUNICATIONS CONDUIT WITH MULETAPE.
3. AT LANDSCAPED AREAS RESTORE SURFACES TO MATCH EXIST ADJACENT SURFACES.
4. 5 MIL THICK ORANGE (TELECOMMUNICATIONS) COLORED PLASTIC WARNING TAPE 75MM WIDE, ENTIRE LENGTH OF DUCT. TAPE TO HAVE CONTINUOUS METALLIC BACKING AND CORROSION RESISTANT FOIL CORE. WARNING AND IDENTIFICATION TO BE IMPRINTED ON TAPE AND SHALL READ "CAUTION BURIED TELECOMMUNICATIONS CABLE BELOW". MESSAGE SHALL RE REPEATED APPROXIMATELY EVERY 3050MM.
5. WHERE ELECTRICAL/COMMUNICATION DUCTLINES CROSS OTHER UTILITIES MAINTAIN MINIMUM 305mm VERTICAL SEPARATION BETWEEN ELECTRICAL/COMMUNICATION DUCTS AND OTHER UTILITIES (GAS, WATER, SEWER, ETC.)

CONCRETE ENCASED DUCT DETAILS

NOTE:

COORDINATE PLACEMENT OF NEW DUCT WHERE IT IS INSTALLED ALONG EXISTING DUCT, AND ENSURE IT TO MEET THE REQUIRED BURIAL DEPTH AND LOCATION OF PENETRATION INTO EXIST MAINTENANCE HOLE.

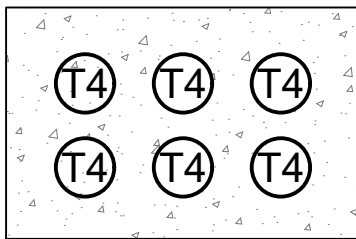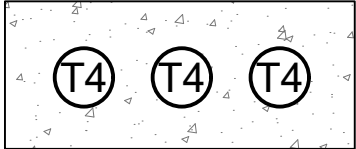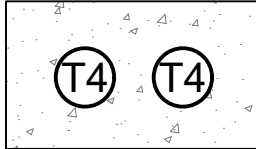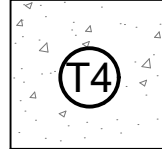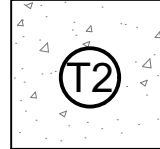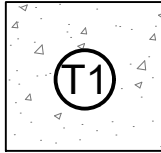				
A	B	C	D	E
				
F				

DUCT SCHEDULE	
TYPE	DESCRIPTION
T4	104C: TELECOM DUCT
T2	53C: TELECOM DUCT
T1	27C: LIGHTING DUCT



**U.S. Army Corps
Engineers®**

[illegible]

JAPAN DISTRICT, OKINAWA AREA OFFICE		SOLICITATION NO.:	
USAED-4, UNIT 35132		DRAWN BY:	
APO, AP 96374-5132		CHECKED BY:	
 SSPM INTERNATIONAL, INC. 501 KALANIANA'OLUHIA DRIVE, #20 HONOLULU, HAWAII 96817		CONTRACT NO.:	
		SCALE: AS SHOWN	
		SUBMITTED BY:	
		SIZE:	FILE NAME:
		ISO A1	

NATIONAL ACADEMY OF SCIENCES
 VEHICLE MAINTENANCE SHOP
 FY20 MCA PN77833
 DUCT SECTION AND DETAILS

SHEET ID

S501

INTERMEDIATE DESIGN

- ① Ø15X600 GROUND RODS, THREADED ENDS WITH WASHER & NUT
- ② GROUNDING FOR EXIST MAINTENANCE HOLES
- ③ GROUNDING FOR NEW MAINTENANCE HOLES




[illegible]

JAPAN DISTRICT, OKINAWA AREA OFFICE USASD-J UNIT 35132 APO, AP 96374-5132		 SSFM INTERNATIONAL, INC 501 SUMMER STREET, SUITE 620	
DRAWN BY:	SOLICITATION NO.:	SUBMITTED BY:	SCALE: AS SHOWN
CHECKED BY:	CONTRACT NO.:	SIZE:	FILE NAME:

MAINTENANCE HOLE DETAILS


SHEET ID

TS503

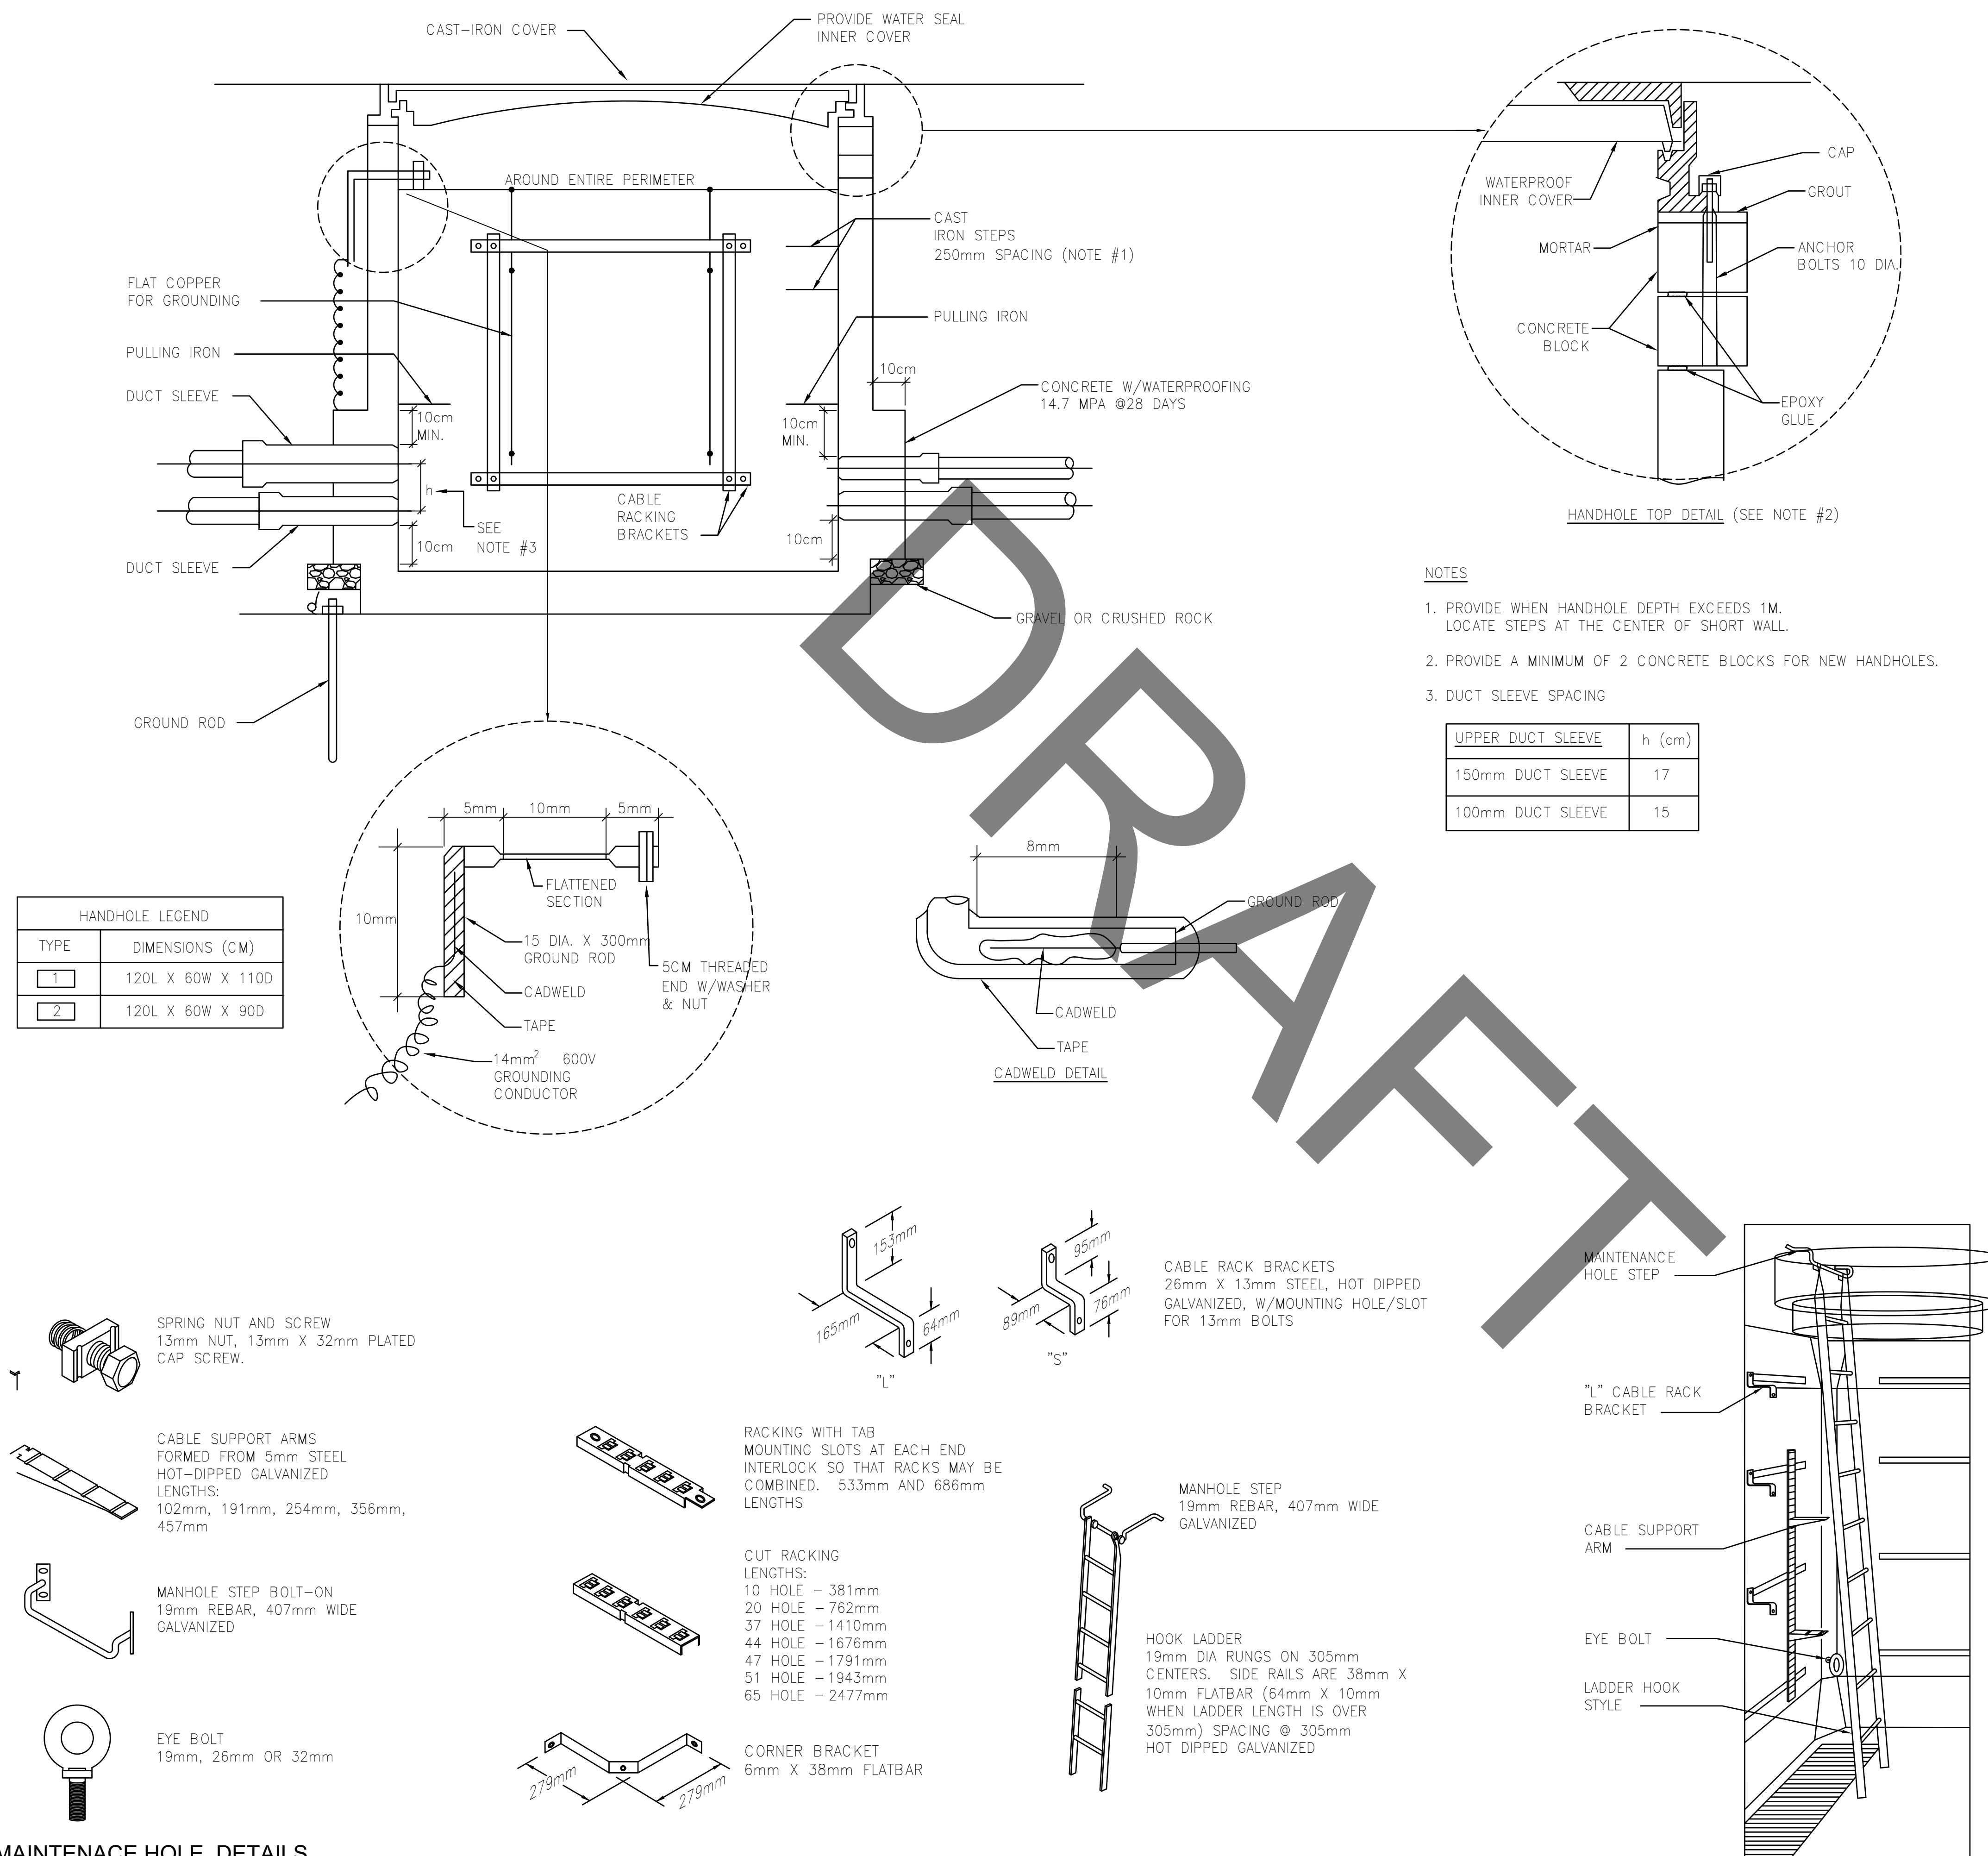

1. ALL HARDWARE SUCH AS LADDER, CABLE RACK, CABLE ARM AND STEP, ETC. SHALL BE GALVANIZED FOR RUST PROTECTION, GALVANIZATION SHALL MEET JIS H8641HDZ35 OR BETTER.

[illegible]

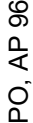
US ARMY CORPS OF ENGINEERS JAPAN DISTRICT, OKINAWA AREA OFFICE UTRICK, 1352 JAGC, AP 96374-132	DESIGNED BY:	ISSUE DATE:
 SOFM INTERNATIONAL, INC 501 SUMNER STREET, SUITE 620	DRAWN BY:	SOLICITATION NO.:
	CHECKED BY:	CONTRACT NO.:
	SUBMITTED BY:	SCALE: AS SHOWN
	SIZE:	FILE NAME:

KADENA AIR BASE, OKINAWA, JAPAN
VEHICLE MAINTENANCE SHOP
FY20 MCA PN77833

SHEET ID

TS511

INTERMEDIATE DESIGN

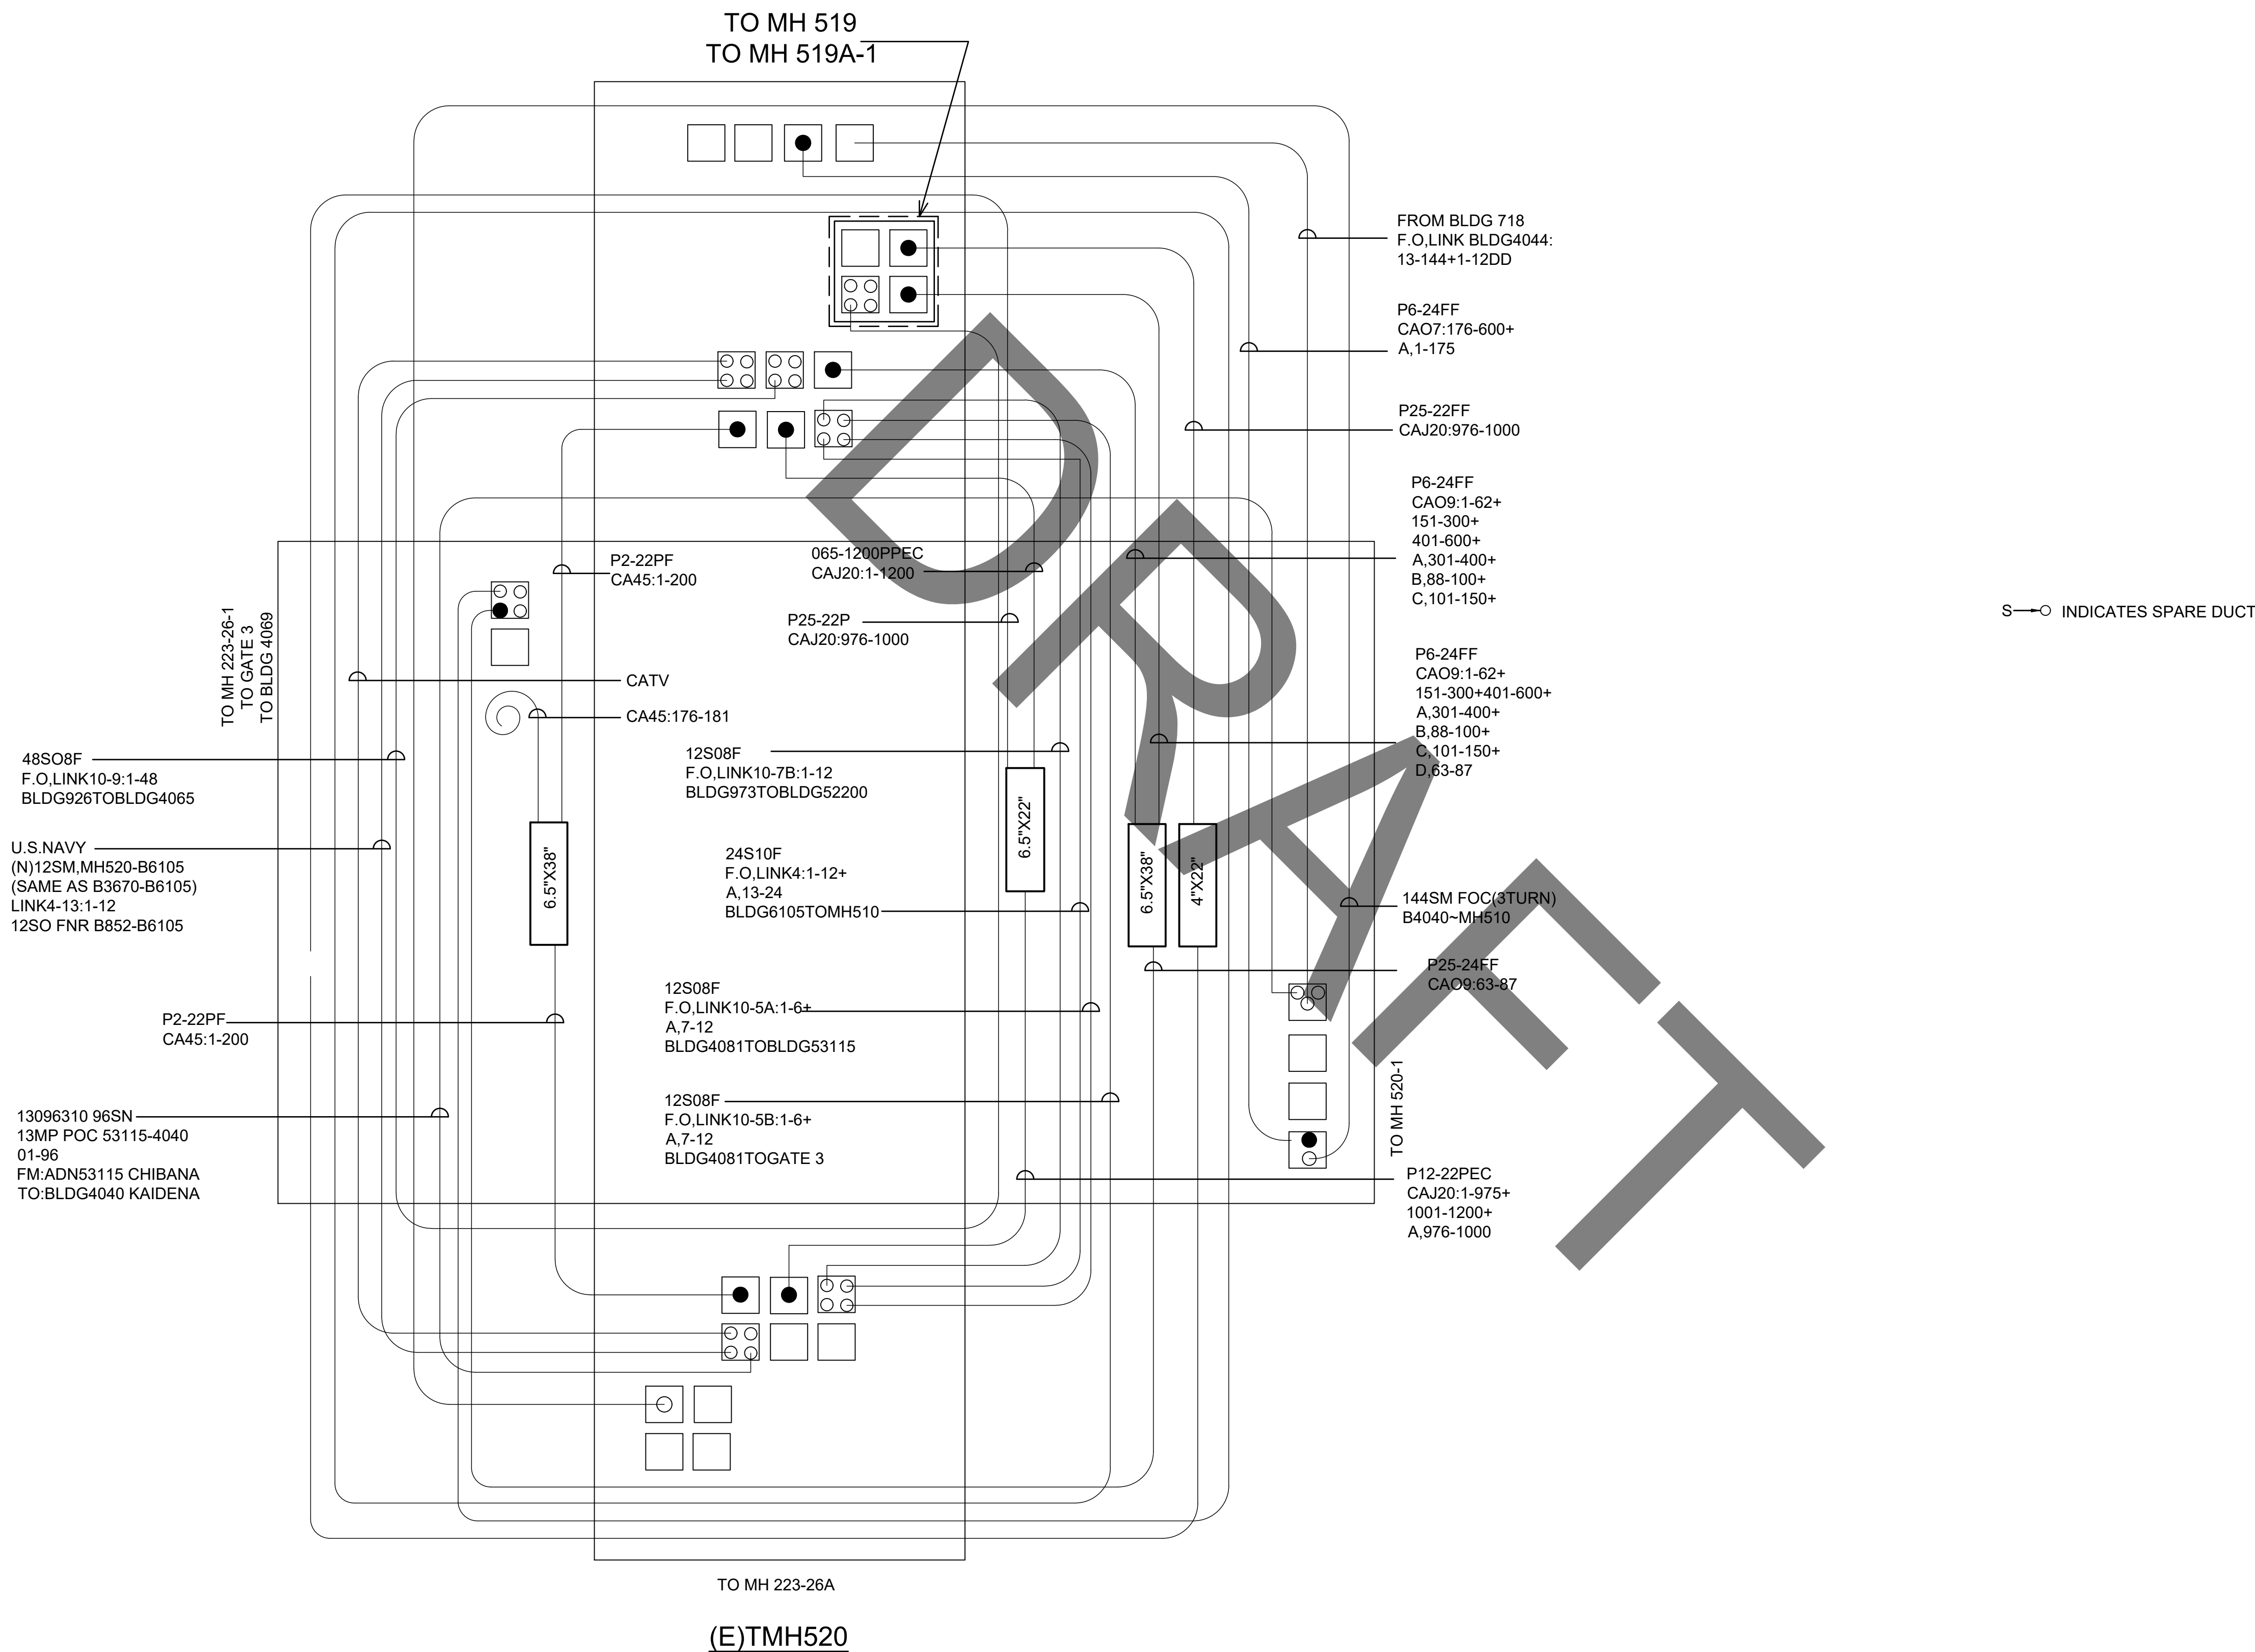

- SITE PREPARATION WORK FOR VMS FACILITIES.
- LOONEY STREET AND ELECTRICAL AND TELECOMMUNICATIONS INFRASTRUCTURE IMPROVEMENTS.
- CONSTRUCTION OF CABLE HUT, RELOCATION OF COMMUNICATIONS HUB FOR CRITICAL OPTICAL FIBER AND COPPER CABLES FROM B4040, AND REESTABLISH THE SERVICES.
- ENSURE THAT TELECOMMUNICATION SERVICES TO EXISTING ADA BUILDINGS (B4040 THRU B4047) ARE MAINTAINED.
- RESTORE OPTICAL FIBER CABLES TO K-SITES FROM NEW CABLE HUT.
- CONSTRUCTION OF VEHICLE MAINTENANCE SHOP, FIRE PUMP HOUSE, WATER STORAGE TANK, AND ASSOCIATED TELECOMMUNICATIONS INFRASTRUCTURE.

- CONSTRUCTION OF ORGANIZATIONAL EQUIPMENT STORAGE, POL STORAGE, AND ASSOCIATED TELECOMMUNICATIONS INFRASTRUCTURE.

- CONSTRUCTION OF ORGANIZATIONAL VEHICLE PARKING LOT.
- CONSTRUCTION OF WASH RACK.

- CONSTRUCTION OF TEMPORARY FACILITIES AT SWING SPACE SITE MUST BE COMPLETED PRIOR TO DEMOLITION OF EXISTING ADA BUILDINGS (B4040 THRU B4047) AND SITE PREPARATION WORK FOR SSA FACILITIES.
- CONSTRUCTION OF NEW SUPPLY SUPPORT ACTIVITY (SSA) WAREHOUSE, STORAGE SHED AND ASSOCIATED TELECOMMUNICATIONS INFRASTRUCTURE.
- CONSTRUCTION OF SSA PARKING LOT.


1. UNDER CLING 0001 THRU 0003, EXISTING SERVICES TO ADA BUILDINGS SHALL BE MAINTAINED WHILE THE CRITICAL FIBER AND COPPER CABLES IN BLDG 4040 WILL BE RELOCATED TO THE NEW CABLE HUT.
2. OPTICAL FIBER CABLES SUPPORTING FO PEDESTALS #1 & #2 AT K-SITES SHALL BE REMOVED AND RESTORED UTILIZING EXISTING AND NEW INFRASTRUCTURE.

- 1 EXIST F CABLE HUB LOCATED IN ADA B4040 MUST BE RELOCATED TO A PROPOSED NEW CABLE HUT AND ALL EXIST CRITICAL SERVICES SHALL BE RE-ESTABLISHED PRIOR TO ANY DEMOLITION WORK.
- 2 EXISTING SERVICES TO ADA BUILDINGS MUST BE MAINTAINED UNDER CLIN 0001 THRU 0003. RECONNECT THE SERVICES TO B4040 FROM THE NEW CABLE HUT.
- 3 REMOVE ALL EXIST FO AND COPPER CABLES SERVING ADA BUILDINGS, INCLUDING THE ASSOCIATED INFRASTRUCTURE UNDER CLIN 0004.
- 4 EXIST OPTICAL FIBER CABLES SERVING THE FO PEDESTALS AT K-SITES REMOVED AND RE-INSTALLED FROM THE NEW CABLE HUT.
- 5 EXIST MAINTENANCE HOLE TO REMAIN. MODIFY EXIST MAINTENANCE HOLE FINISH TO MATCH THE FINISH GRADE AS REQUIRED.
- 6 DEMOLISH EXIST INFRASTRUCTURE AFTER FO AND COPPER CABLES ARE REMOVED.



US Army Corps
of Engineers®

[illegible]

 US ARMY CORPS OF ENGINEERS JAPAN DISTRICT, OKINAWA AREA OFFICE USAED-J, UNIT 35132 APO, AP 96374-5132		DESIGNED BY: DRAWN BY: CHECKED BY: SUBMITTED BY: SCALE: HAS SHOWIN	ISSUE DATE: SOLICITATION NO.: CONTRACT NO.: FILE NAME: SIZE: A0 A1
 SSEW INTERNATIONAL, INC. 507 SUMNER STREET, SUITE 620 HONOLULU, HAWAII 96817			

KADENA AIR BASE OKINAWA, JAPAN
VEHICLE MAINTENANCE SHOP
FY20 MCA PN77833

- SITE PREPARATION WORK FOR VMS FACILITIES.
- LOONEY STREET AND ELECTRICAL AND TELECOMMUNICATIONS INFRASTRUCTURE IMPROVEMENTS.
- CONSTRUCTION OF CABLE HUT, RELOCATION OF COMMUNICATIONS HUB FOR CRITICAL OPTICAL FIBER AND COPPER CABLES FROM B4040, AND REESTABLISH THE SERVICES.
- ENSURE THAT TELECOMMUNICATION SERVICES TO EXISTING ADA BUILDINGS (B4040 THRU B4047) ARE MAINTAINED.
- RESTORE OPTICAL FIBER CABLES TO K-SITES FROM NEW CABLE HUT.
- CONSTRUCTION OF VEHICLE MAINTENANCE SHOP, FIRE PUMP HOUSE, WATER STORAGE TANK, AND ASSOCIATED TELECOMMUNICATIONS INFRASTRUCTURE.

- CONSTRUCTION OF ORGANIZATIONAL EQUIPMENT STORAGE, POL STORAGE, AND ASSOCIATED TELECOMMUNICATIONS INFRASTRUCTURE.

- CONSTRUCTION OF ORGANIZATIONAL VEHICLE PARKING LOT.
- CONSTRUCTION OF WASH RACK.

- CONSTRUCTION OF TEMPORARY FACILITIES AT SWING SPACE SITE MUST BE COMPLETED PRIOR TO DEMOLITION OF EXISTING ADA BUILDINGS (B4040 THRU B4047) AND SITE PREPARATION WORK FOR SSA FACILITIES.
- CONSTRUCTION OF NEW SUPPLY SUPPORT ACTIVITY (SSA) WAREHOUSE, STORAGE SHED AND ASSOCIATED TELECOMMUNICATIONS INFRASTRUCTURE.
- CONSTRUCTION OF SSA PARKING LOT.

1. UNDER CLING 0001 THRU 0003, EXISTING SERVICES TO ADA BUILDINGS SHALL BE MAINTAINED WHILE THE CRITICAL FIBER AND COPPER CABLES IN BLDG 4040 WILL BE RELOCATED TO THE NEW CABLE HUT.
2. OPTICAL FIBER CABLES SUPPORTING FO PEDESTALS #1 & #2 AT K-SITES SHALL BE REMOVED AND RESTORED UTILIZING EXISTING AND NEW INFRASTRUCTURE.

[illegible]

KADENA AIR BASE, OKINAWA, JAPAN
VEHICLE MAINTENANCE SHOP
FY20 MCA PN77833

TELECOM DISTRIBUTION DIAGRAM (CLIN 0001 - CLIN 0003)

SHEET ID
TS611

- 1 EXIST FO CABLE HUB LOCATED IN ADA B4040 MUST BE RELOCATED TO A PROPOSED NEW CABLE HUT AND ALL EXIST CRITICAL SERVICES SHALL BE RE-ESTABLISHED PRIOR TO ANY DEMOLITION WORK.
- 2 EXISTING SERVICES TO ADA BUILDINGS MUST BE MAINTAINED UNDER CLIN 0001 THRU 0003. RECONNECT THE SERVICES TO B4040 FROM THE NEW CABLE HUT.
- 3 EXIST OPTICAL FIBER CABLES SERVING THE FO PEDESTALS AT K-SITES REMOVED AND RE-INSTALLED FROM THE NEW CABLE HUT.
- 4 EXIST MAINTENANCE HOLE TO REMAIN. MODIFY EXIST MAINTENANCE HOLE FINISH TO MATCH THE FINISH GRADE AS REQUIRED.
- 5 PROVIDE NEW DUCTS UTILIZING EXISTING MAINTENANCE HOLES TO SUPPORT THE NEW FACILITIES.



CLIN 0001:

- SITE PREPARATION WORK FOR VMS FACILITIES.
- LOONEY STREET AND ELECTRICAL AND TELECOMMUNICATIONS INFRASTRUCTURE IMPROVEMENTS.
- CONSTRUCTION OF CABLE HUT, RELOCATION OF COMMUNICATIONS HUB FOR CRITICAL OPTICAL FIBER AND COPPER CABLES FROM B4040, AND REESTABLISH THE SERVICES.
- ENSURE THAT TELECOMMUNICATION SERVICES TO EXISTING ADA BUILDINGS (B4040 THRU B4047) ARE MAINTAINED.
- RESTORE OPTICAL FIBER CABLES TO K-SITES FROM NEW CABLE HUT.
- CONSTRUCTION OF VEHICLE MAINTENANCE SHOP, FIRE PUMP HOUSE, WATER STORAGE TANK, AND ASSOCIATED TELECOMMUNICATIONS INFRASTRUCTURE.

CLIN 0002:

- CONSTRUCTION OF ORGANIZATIONAL EQUIPMENT STORAGE, POL STORAGE, AND ASSOCIATED TELECOMMUNICATIONS INFRASTRUCTURE.

CLIN 0003:

- CONSTRUCTION OF ORGANIZATIONAL VEHICLE PARKING LOT.
- CONSTRUCTION OF WASH RACK.

CLIN 0004

- CONSTRUCTINO OF TEMPORARY FACILITIES AT SWING SPACE SITE MUST BE COMPLETED PRIOR TO DEMOLITION OF EXISTING ADA BUILDINGS (B4040 THRU B4047) AND SITE PREPARATION WORK FOR SSA FACILITIES.
- CONSTRUCTION OF NEW SUPPLY SUPPORT ACTIVITY (SSA) WAREHOUSE, STORAGE SHED AND ASSOCIATED TELECOMMUNICATIONS INFRASTRUCTURE.
- CONSTRUCTION OF SSA PARKING LOT.

(E)FO
PEDESTAL #1

(E)TMH-3A

(E)TH

TELECOMMUNICATIONS DISTRIBUTION DIAGRAM - (CLIN0004)

- ## CLIN 0004
- CONSTRUCTION OF TEMPORARY FACILITIES AT SWING SPACE SITE MUST BE COMPLETED PRIOR TO DEMOLITION OF EXISTING ADA BUILDINGS (B4040 THRU B4047) AND SITE PREPARATION WORK FOR SSA FACILITIES.
 - CONSTRUCTION OF NEW SUPPLY SUPPORT ACTIVITY (SSA) WAREHOUSE, STORAGE SHED AND ASSOCIATED TELECOMMUNICATIONS INFRASTRUCTURE.
 - CONSTRUCTION OF SSA PARKING LOT.

KEY NOTES:


- 1 INTERCEPT EXISTING STUB OUTS AND EXTEND NEW DUCT LINES FROM (E)TMH-A TO SSA FACILITIES.
- 2 PROVIDE OPTICAL FIBER AND COPPER CABLES FROM CABLE HUT TO SSA BUILDING, UTILIZING EXISTING AND NEW INFRASTRUCTURE.
- 3 EXISTING SERVICES TO ADA BUILDINGS MUST BE MAINTAINED UNDER CLIN 0001 THRU 0003. RECONNECT THE SERVICES TO B4040 FROM THE NEW CABLE HUT.
- 4 EXTEND TELECOM SERVICE TO STORAGE BUILDING FROM SSA BUILDING.



INTERMEDIATE DESIGN

P
—
O
—
N
—
M
—
L
—
K
—
J
—
I
—
H
—
G
—
F
—
E
—
D
—
C
—
B
—
A

INTERMEDIATE DESIGN

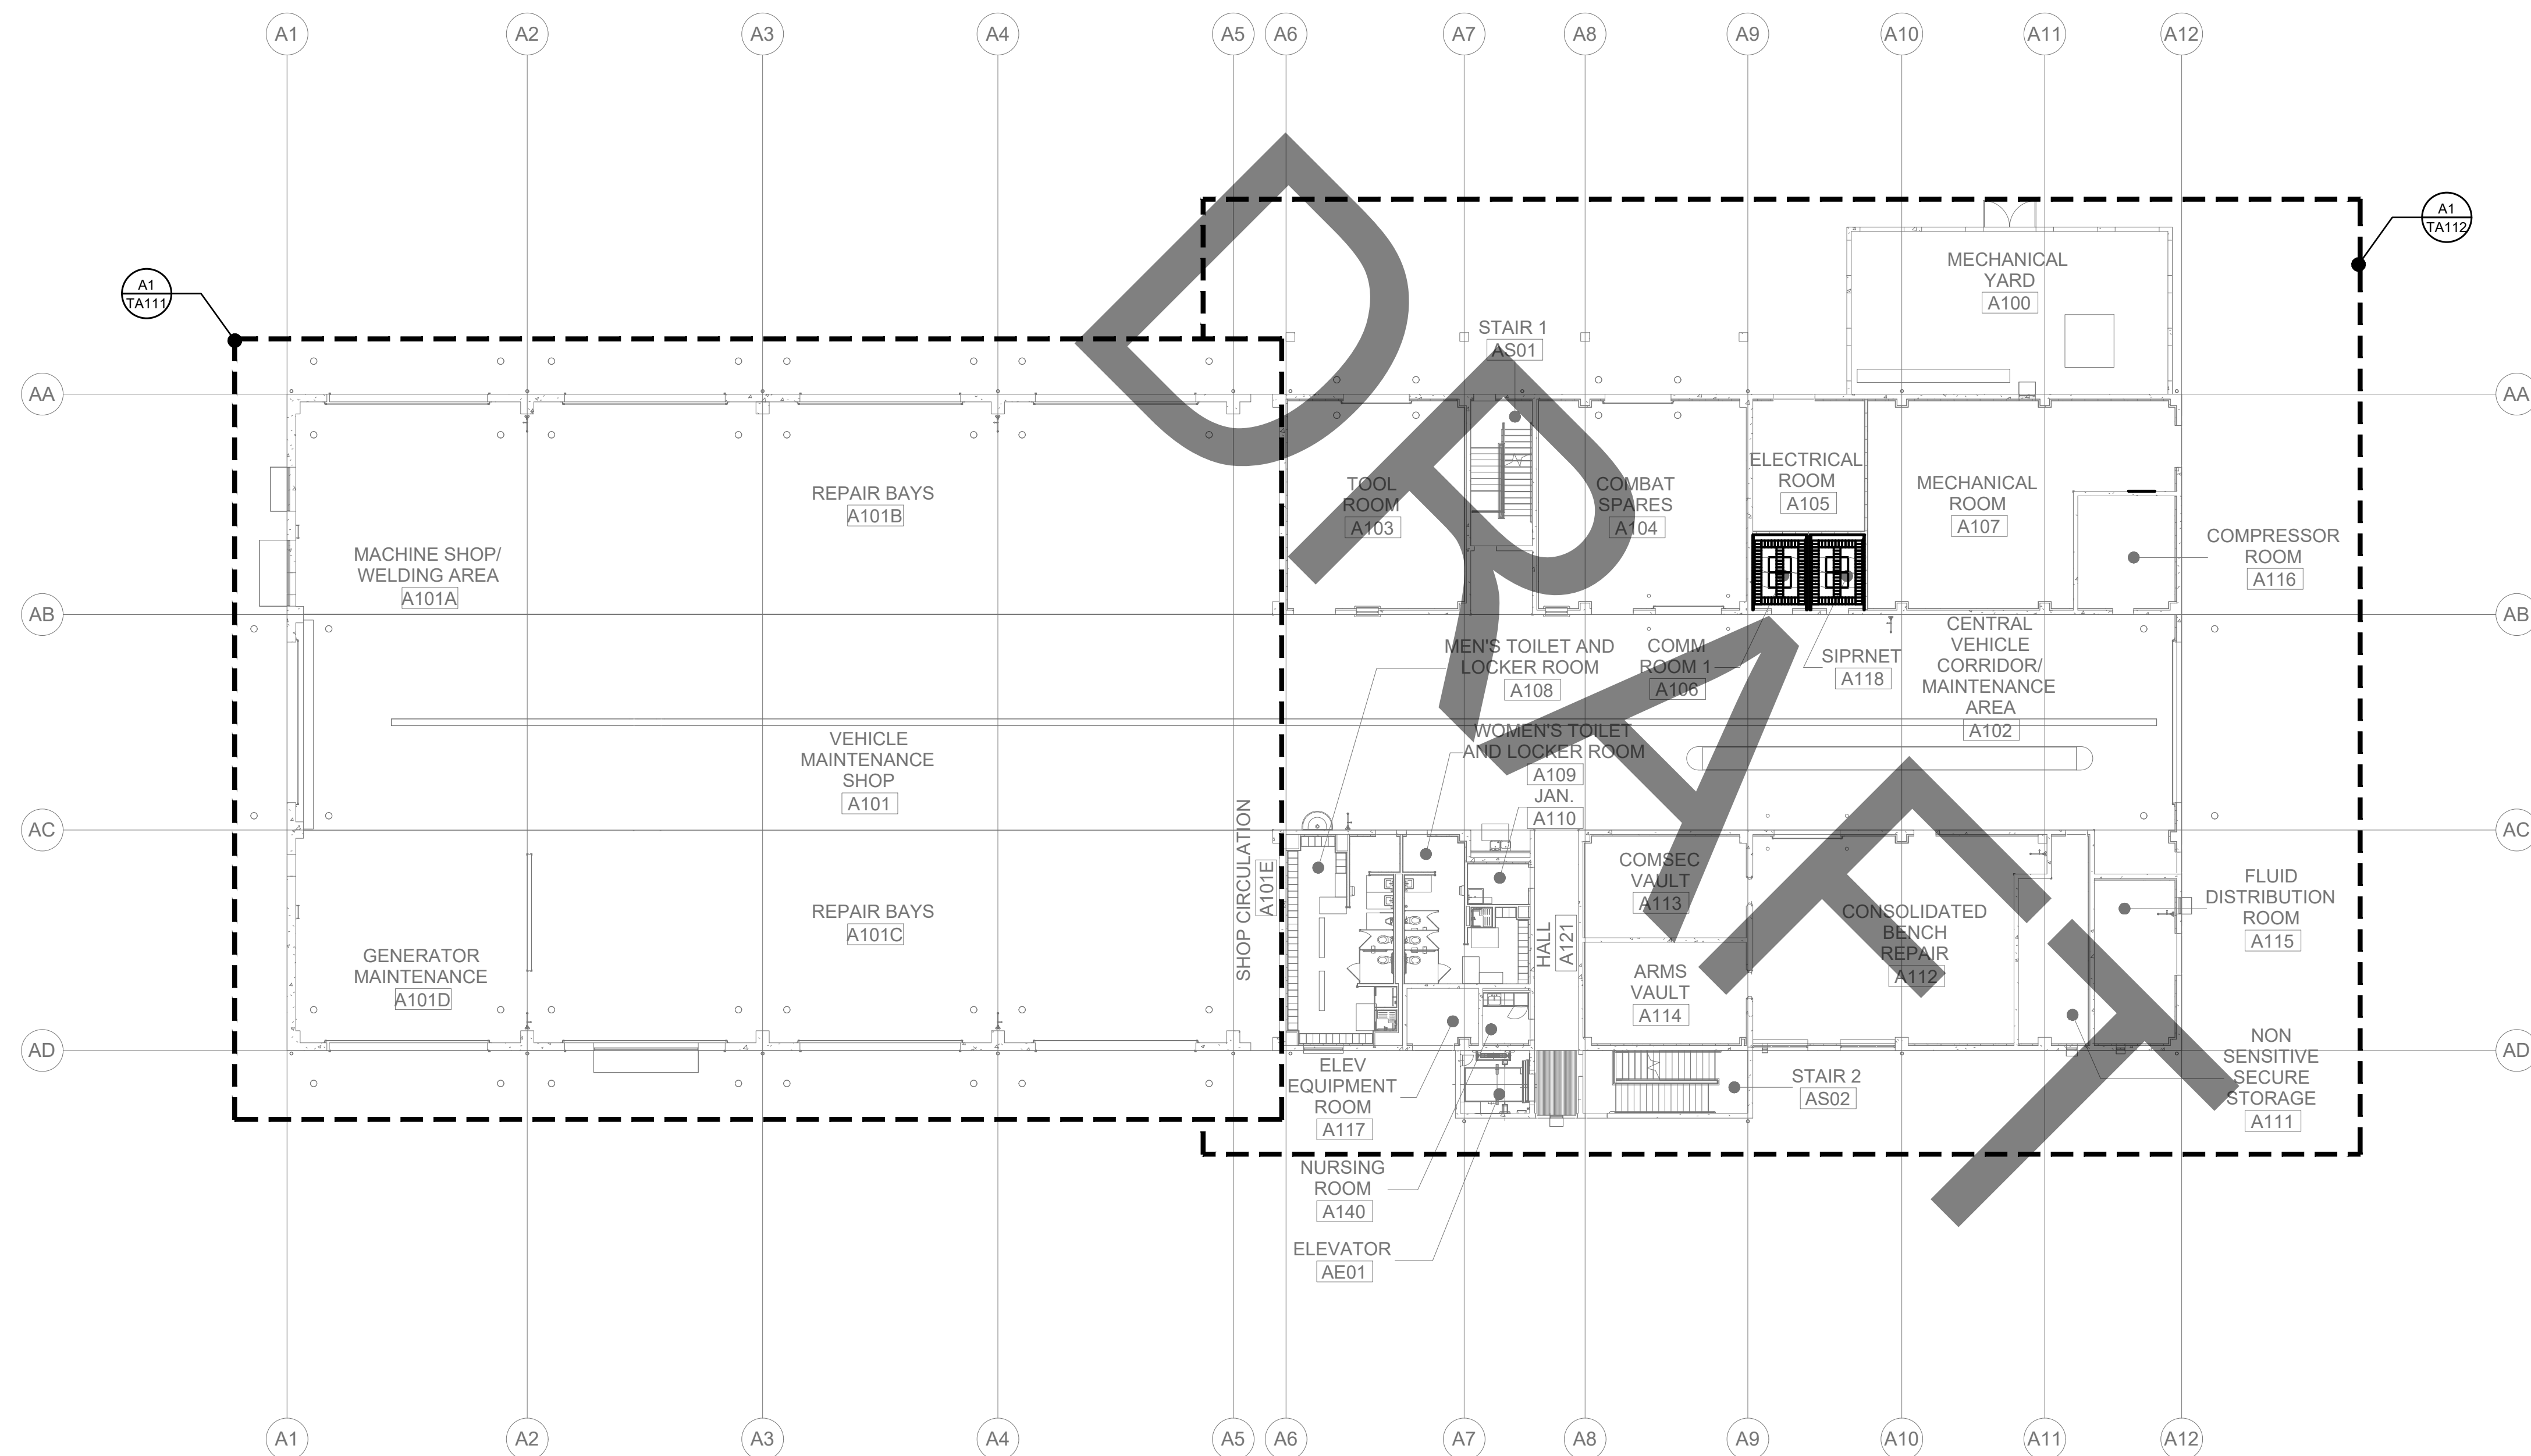

A1 VMS - OVERALL FIRST FLOOR PLAN (CLIN 0001)

GENERAL NOTES

US Army Corps
of Engineers®

Item	Value	Unit
1. 1000	1000	1000
2. 1000	1000	1000
LEGEND

SSPM INTERNATIONAL SSPM INTERNATIONAL, INC 501 SUMNER STREET, SUITE 620	DESIGNED BY:	ISSUE DATE:
	DRAWN BY:	SOLICITATION NO.:
	CHECKED BY:	CONTRACT NO.:
	SUBMITTED BY:	SCALE:
	SIZE:	FILE NAME:

KADENA AIR BASE, OKINAWA, JAPAN
VEHICLE MAINTENANCE SHOP
FY20 MCA PN77833

SHEET ID


TA101

INTERMEDIATE DESIGN

CLIN 0001

KEY PLAN


VMS - LEVEL 1
N.T.S.

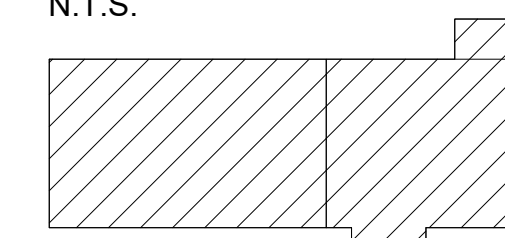


GRAPHIC SCALE




SCALE: 1 : 200

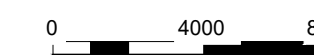

ALL DIMENSIONS AND/OR DIMENSIONS SHOWN IN
CALLOUT/ NOTES ARE IN MILLIMETERS UNLESS
OTHERWISE NOTED.

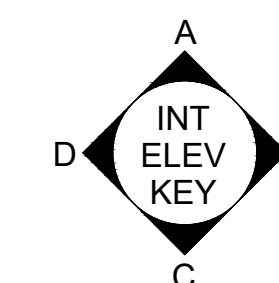

4.400

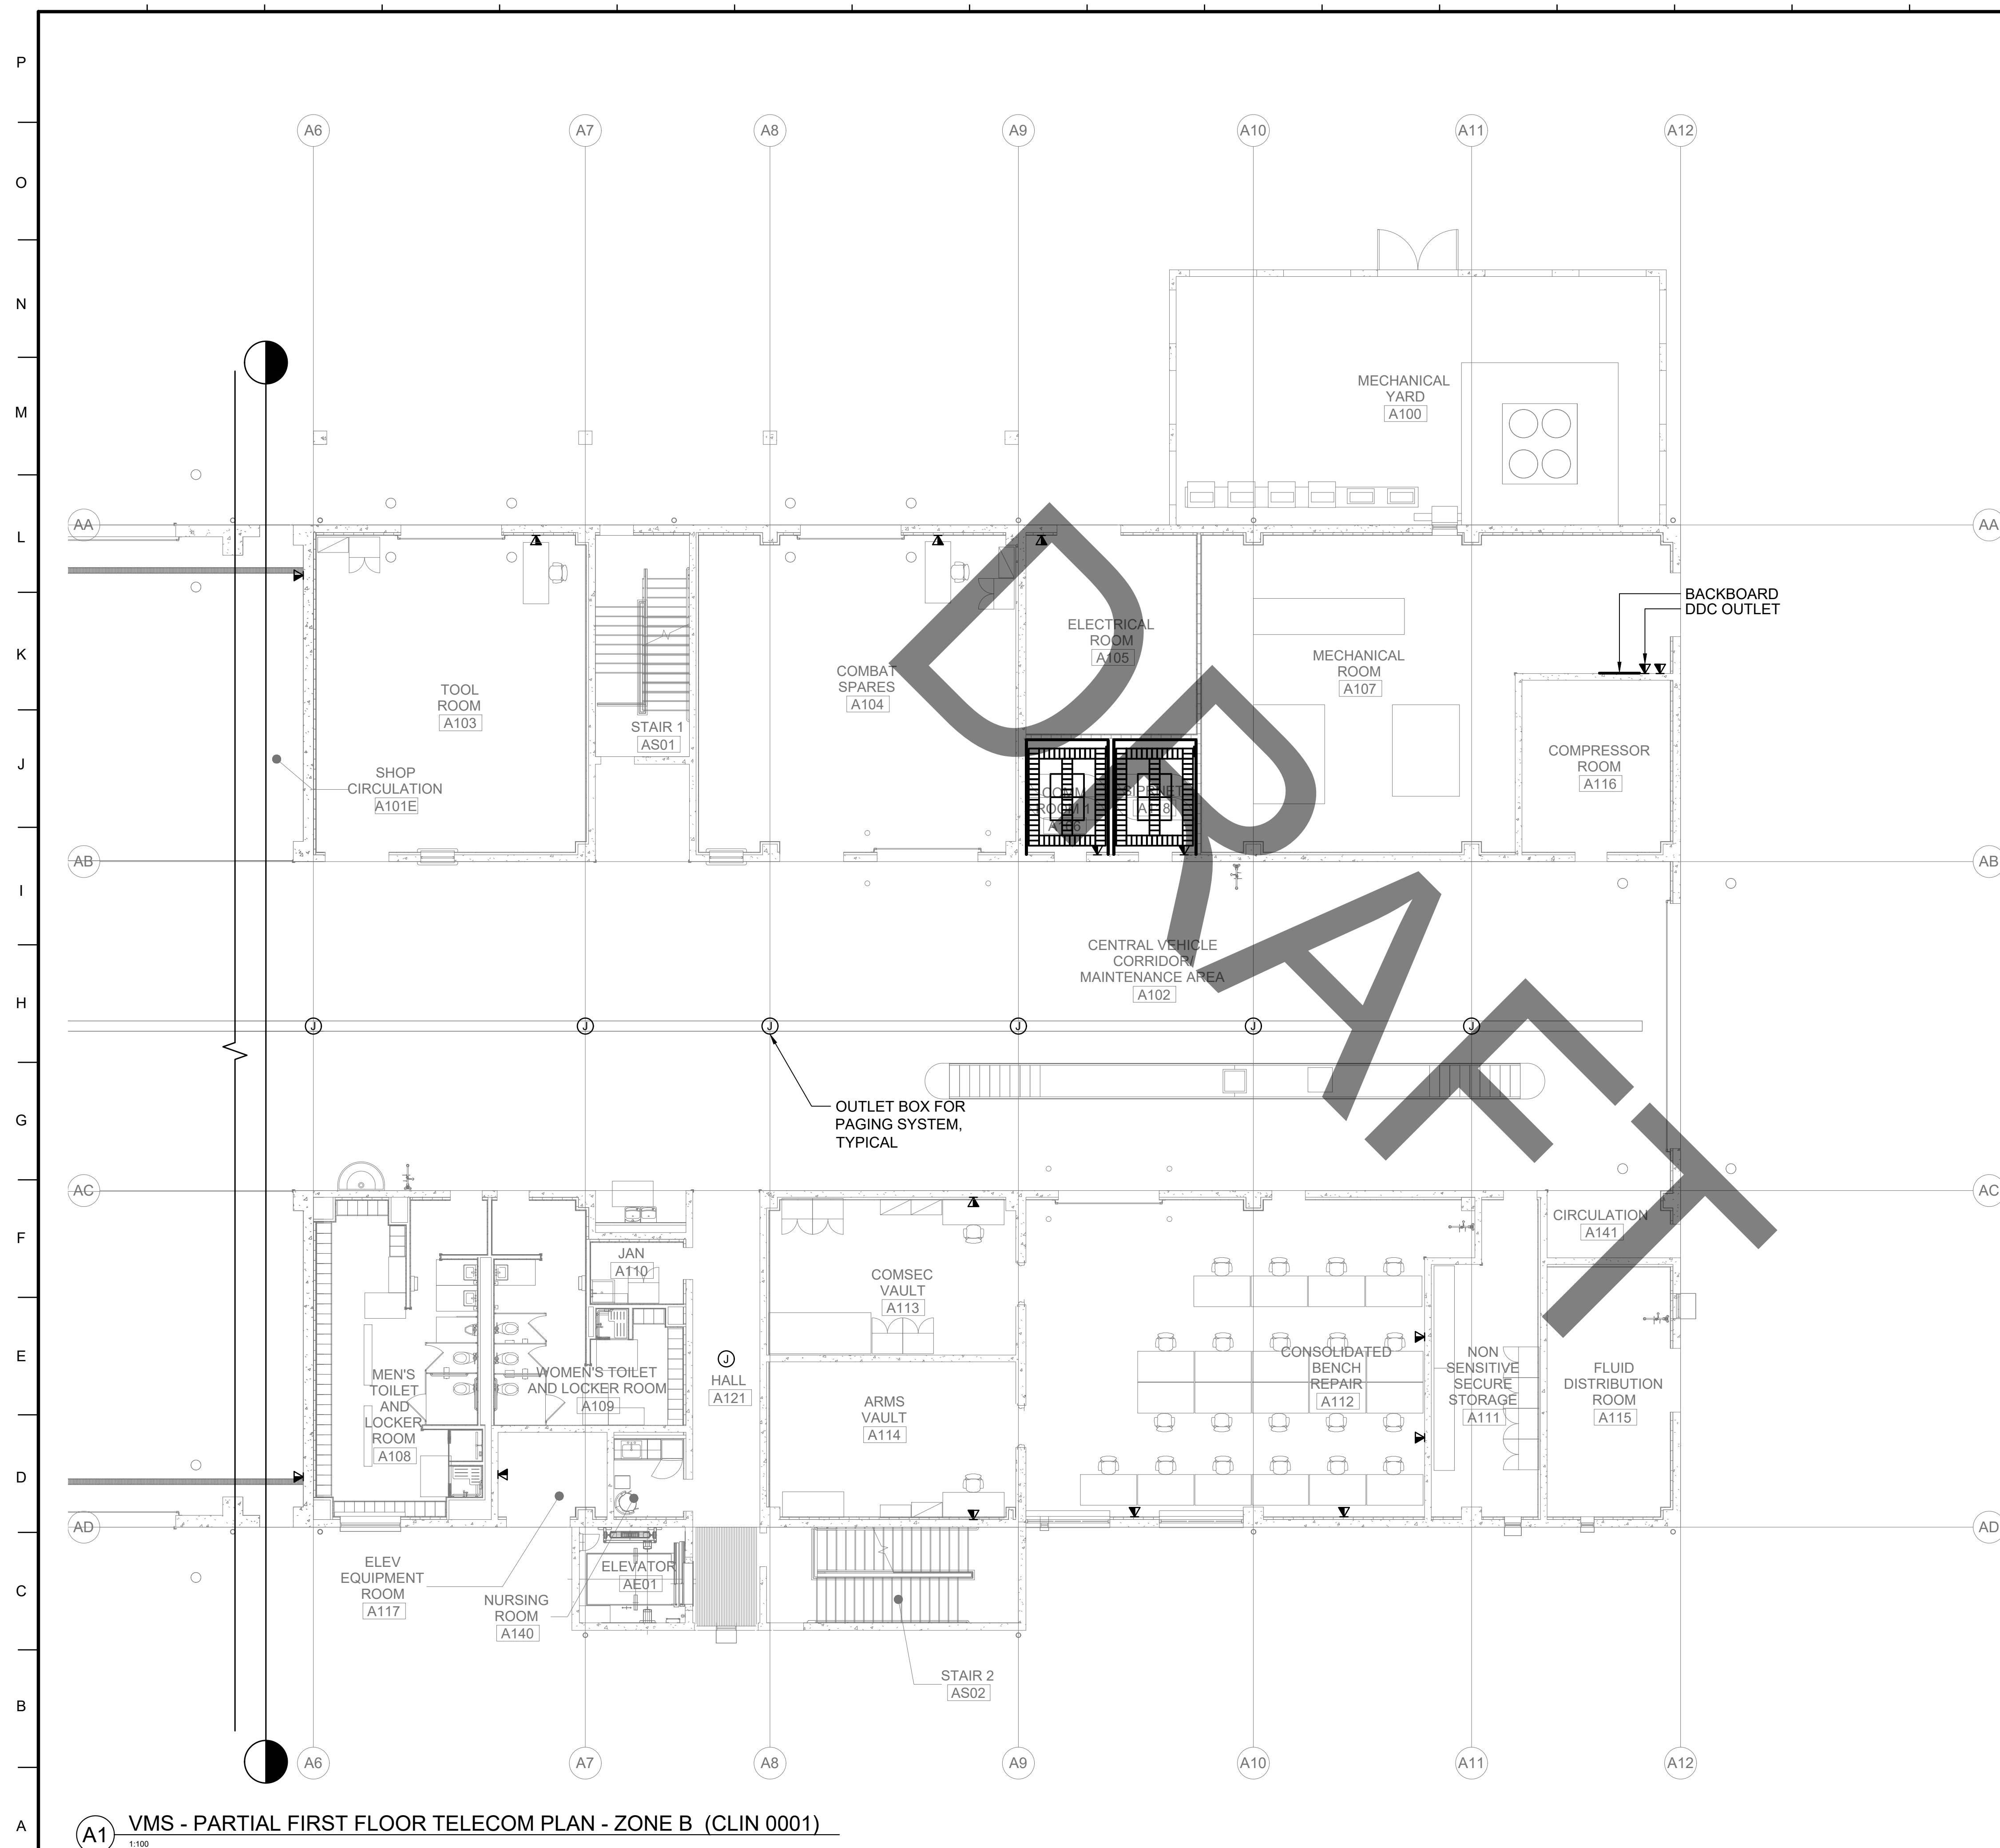

GENERAL NOTES


US Army Corps
of Engineers®

LEGEND


CLIN 0001

KEY PLAN


VMS - LEVEL 1
N.T.S.

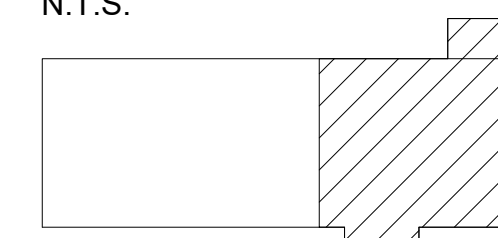

GRAPHIC SCALE

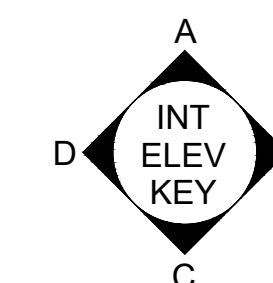

PLAN
NORTH

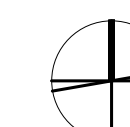

SCALE: 1 : 100

ALL DIMENSIONS AND/OR DIMENSIONS SHOWN IN
CALLOUT/ NOTES ARE IN MILLIMETERS UNLESS
OTHERWISE NOTED.

US ARMY CORPS OF ENGINEERS
JAPAN DISTRICT, OKINAWA AREA OFFICE

USAED-J, UNIT 35132
APO. AP 96374-5132

SSFM
International
SSFM INTERNATIONAL, INC.
401 SUMNER STREET, SUITE 620

VMS - PARTIAL FIRST FLOOR TELECOM PLAN - ZONE B (CLIN 00001)

SHEET ID

TA112

INTERMEDIATE DESIGN

GENERAL NOTES



**U.S. Army Corps
Engineers®**

[illegible]


JAPAN DISTRICT, OKINAWA AREA OFFICE		SOLICITATION NO.:	
USAD-J Unit 35132		DRAWN BY:	
APO, AP 96374-15132		CHECKED BY:	
 SSM INTERNATIONAL, INC. 500 KALANIANAʻOHE BLVD, SUITE 220 HONOLULU, HAWAII 96817		CONTRACT NO.:	
		SUBMITTED BY:	
		AS SHOWN	
ISO A1	SIZE:	FILE NAME:	

VEHICLE MAINTENANCE SHOP
FY20 MCA PN77833


SHEET ID

A401

INTERMEDIATE DESIGN

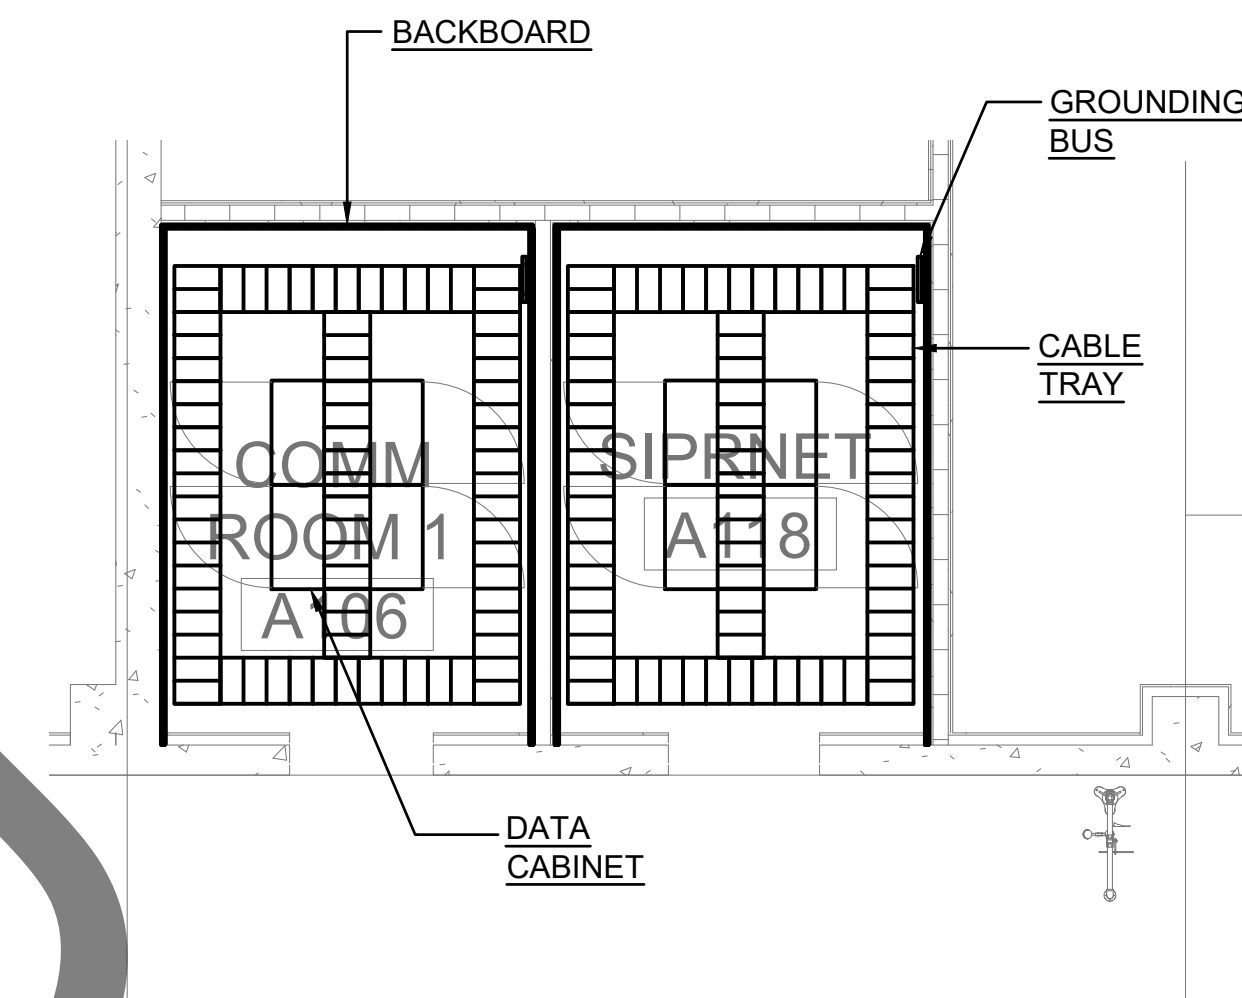

K10 1ST FLOOR COMM ROOM

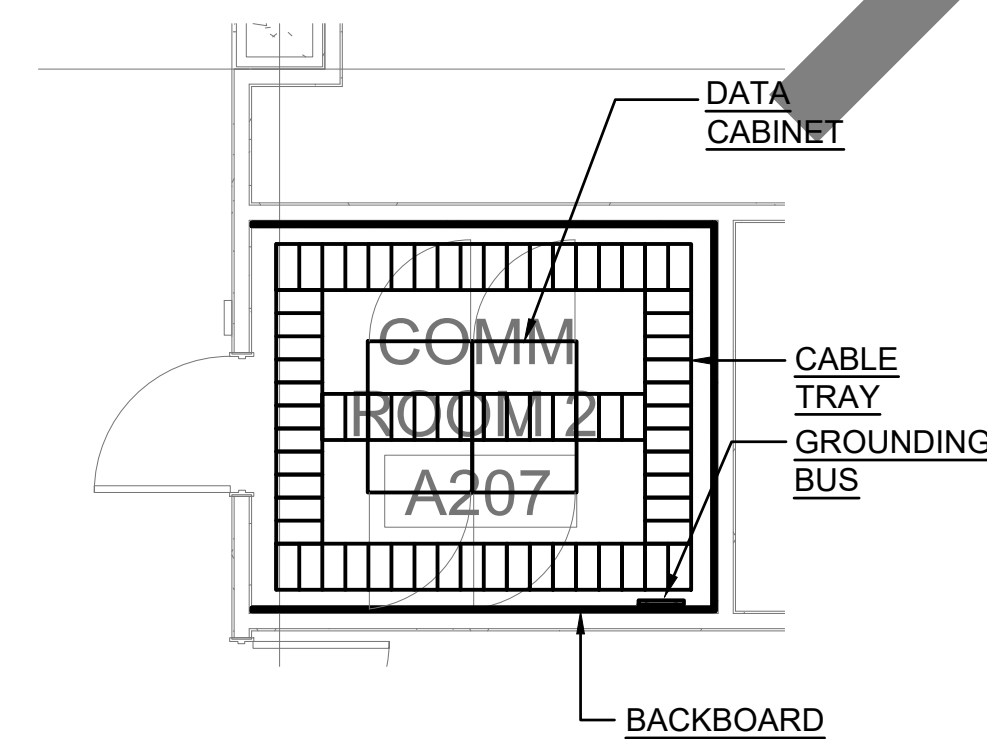

C10 2ND FLOOR ELEC AND COMM ROOM

CLIN 0001

GRAPHIC SCALE



SCALE: 1 : 50



ALL DIMENSIONS AND/OR DIMENSIONS SHOWN IN
CALLOUT/ NOTES ARE IN MILLIMETERS UNLESS
OTHERWISE NOTED.


[illegible]

JAPAN DISTRICT, OKINAWA AREA OFFICE USAED-J UNIT 35132 APO, AP 96374-5132	SSM international	SSM INTERNATIONAL, INC 501 SUMMER STREET, SUITE 620
	DRAWN BY:	SOLICITATION NO.:
	CHECKED BY:	CONTRACT NO.:
	SUBMITTED BY:	SCALE: AS SHOWN
SIZE:	FILE NAME:	

MADEIRA AIR BASE, ORINAWA, JAPAN
VEHICLE MAINTENANCE SHOP
FY20 MCA PN77833

SHEET ID
TA60

INTERMEDIATE DESIGN

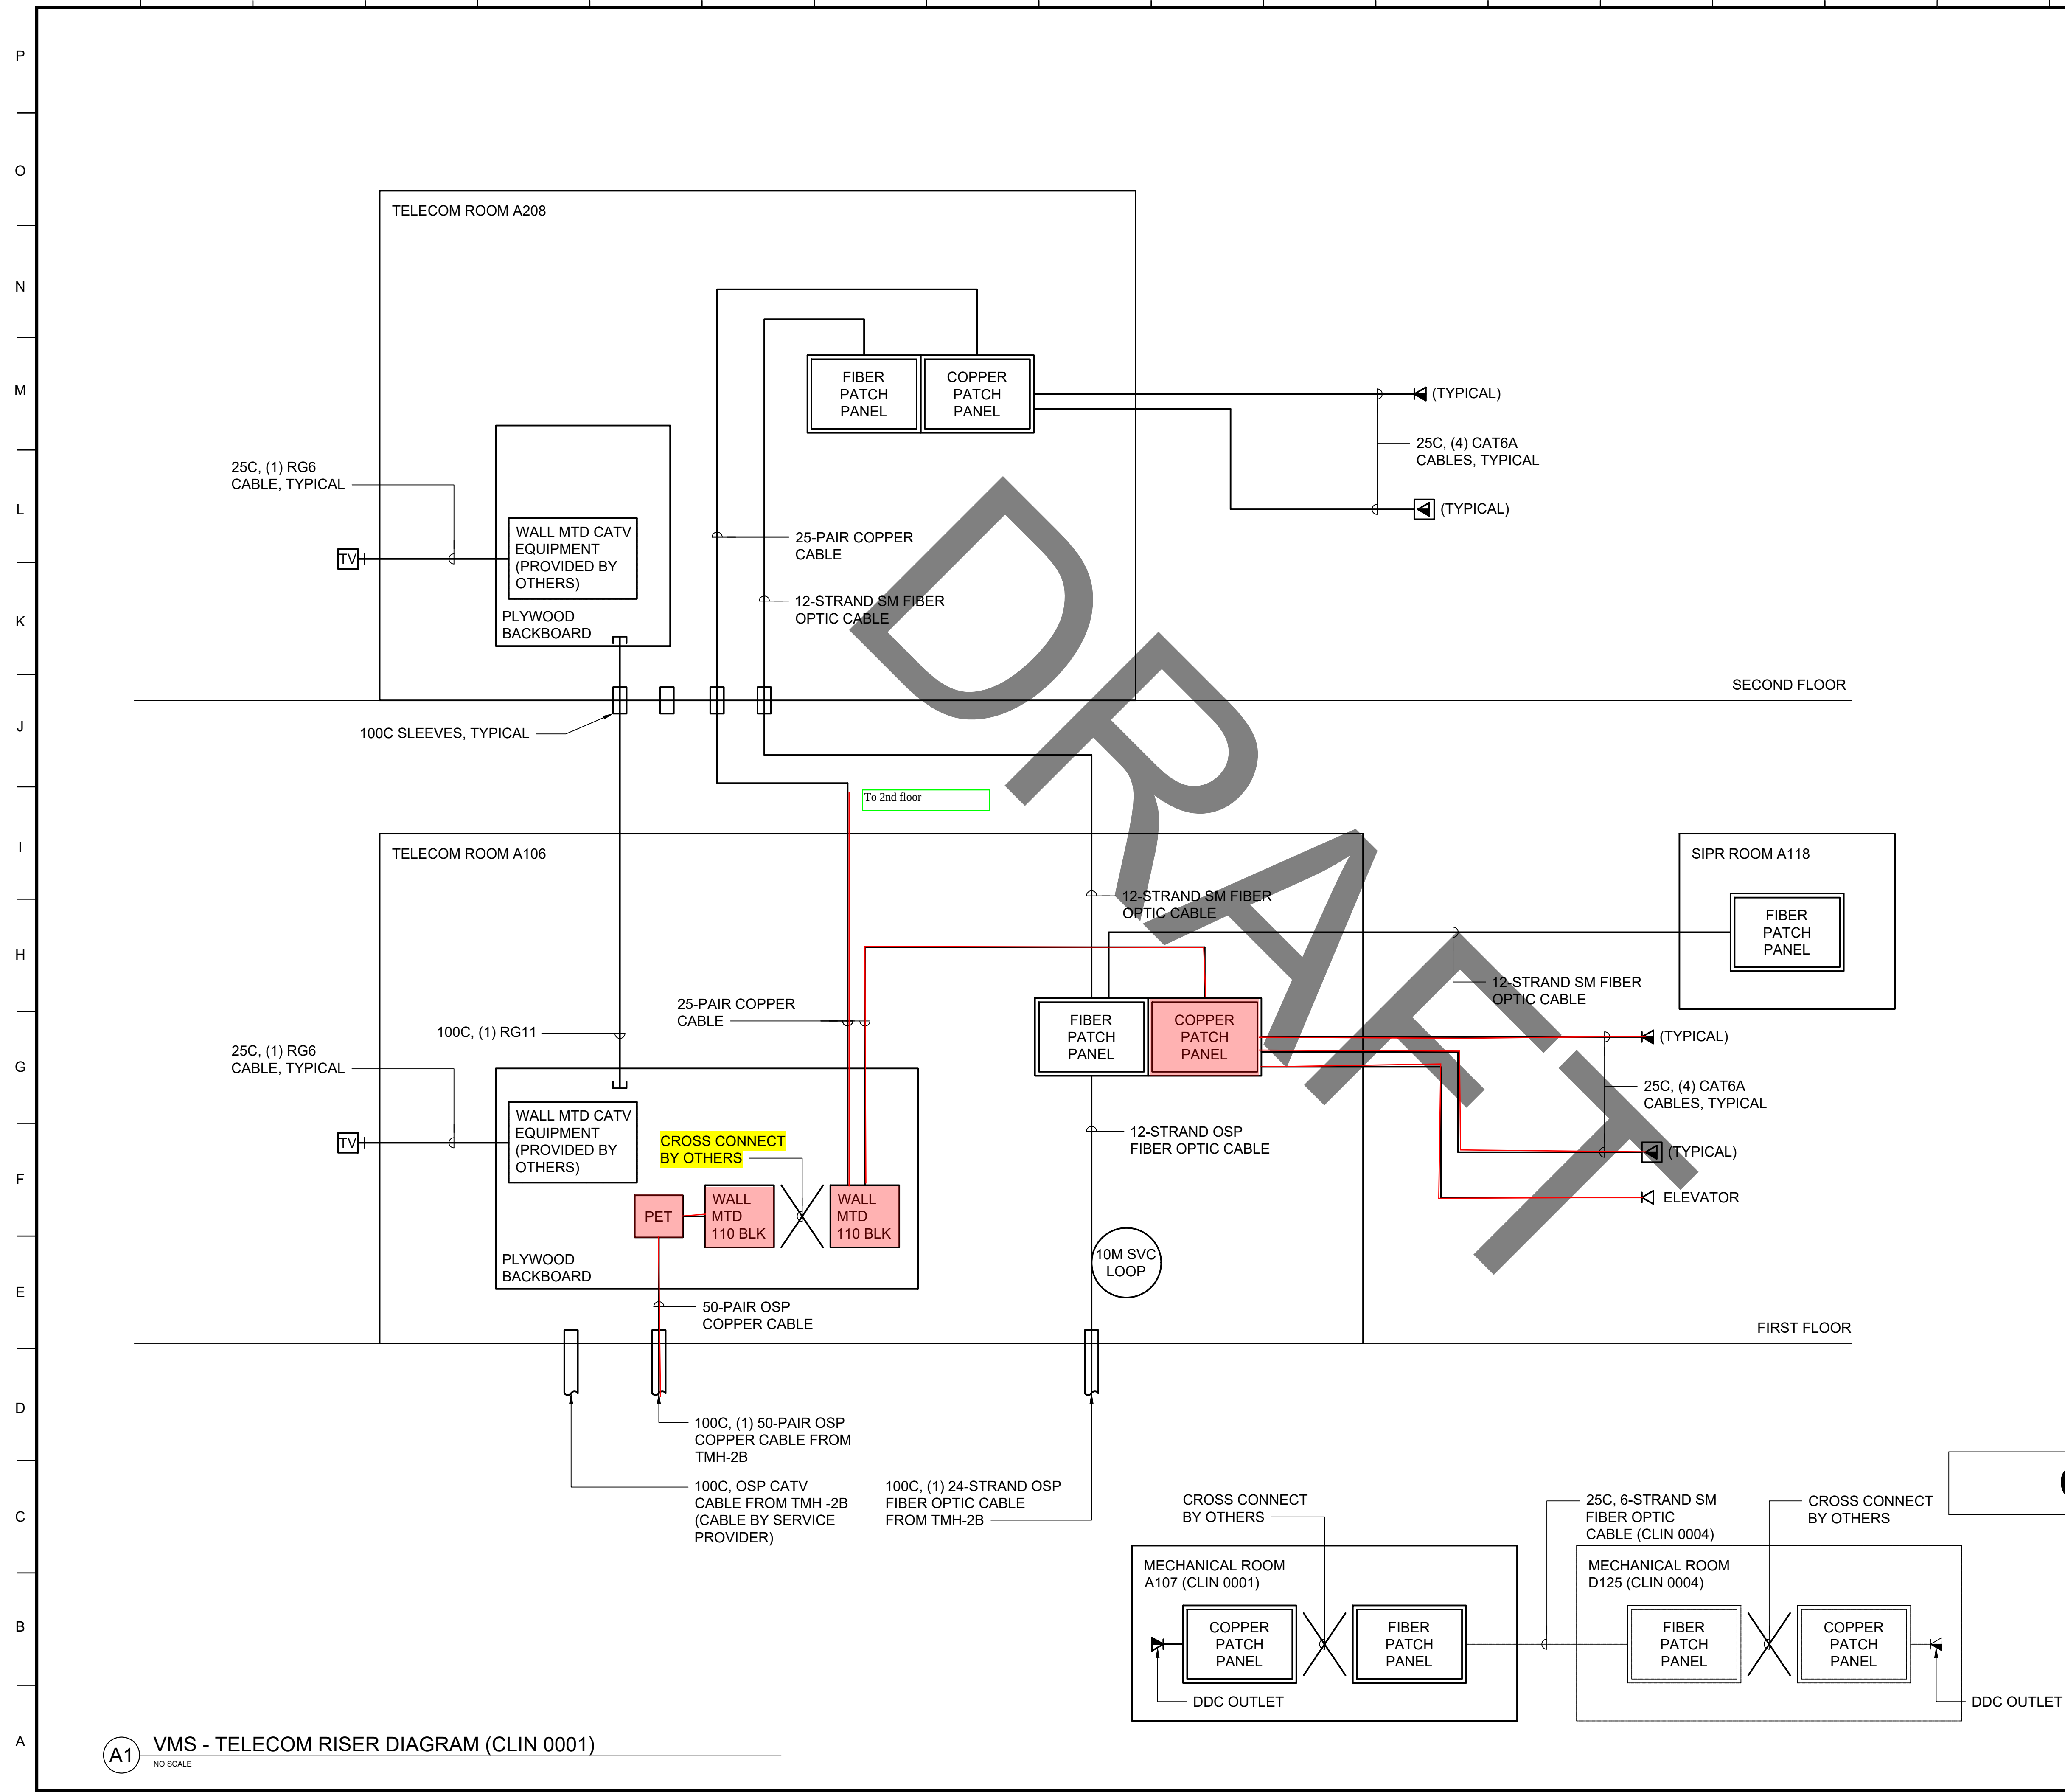

GENERAL NOTES




US Army Corps
of Engineers®

[illegible]

DESIGNED BY:	ISSUE DATE:
DRAWN BY:	SOLICITATION NO.:
CHECKED BY:	CONTRACT NO.:
SUBMITTED BY:	SCALE: AS SHOWN
SIZE: 1/8" x 1/2"	FILE NAME:

US ARMY CORPS OF ENGINEERS
JAPAN DISTRICT, OKINAWA AREA OFFICE
USAE-J, UNIT 35132
APO, AP 96374-5132

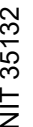

SSFM INTERNATIONAL, INC
501 SUMNER STREET, SUITE 620


KADENA AIR BASE, OKINAWA, JAPAN
VEHICLE MAINTENANCE SHOP
FY20 MCA PN77833

OS - TELECOM PLAN (CLIN 0002)

SHEET ID

TB101

INTERMEDIATE DESIGN

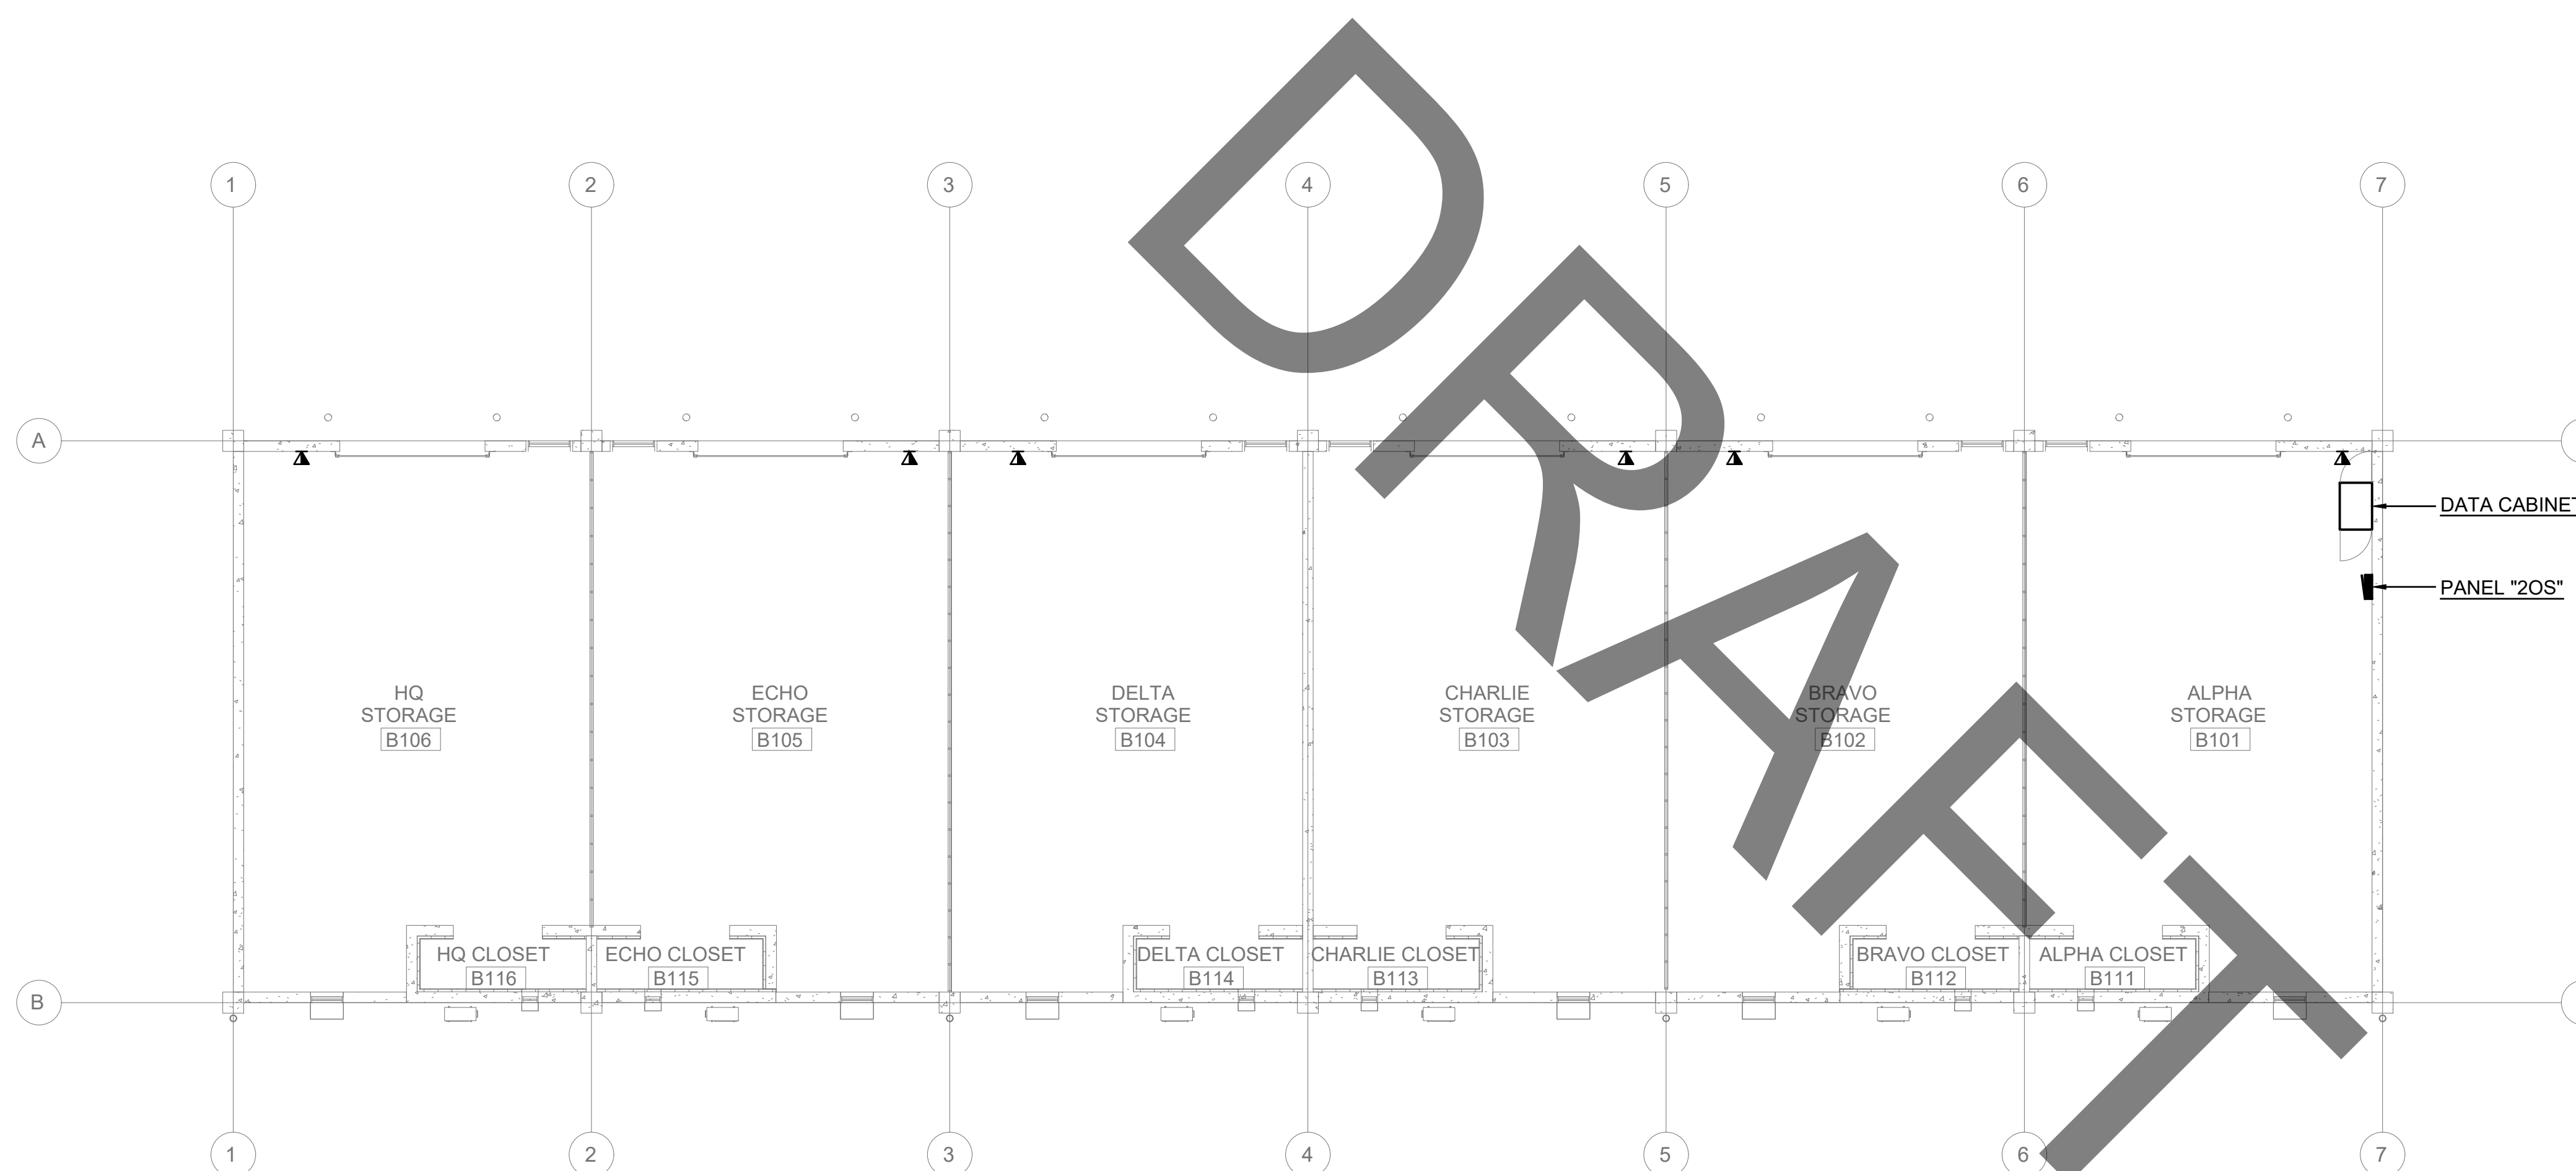

— DATA CABINET

— PANEL "20S"

HQ
STORAGE
B106

ECHO
STORAGE
B105

DELTA
STORAGE
B104

CHARLIE
STORAGE
B103

BRAVO
STORAGE
B102

ALPHA
STORAGE
B101

HQ CLOSET
B116

ECHO CLOSET
B115

DELTA CLOSET
B114


CHARLIE CLOSET
B113

BRAVO CLOSET
B112

ALPHA CLOSET
B111

CLIN 0002

GRAPHIC SCALE

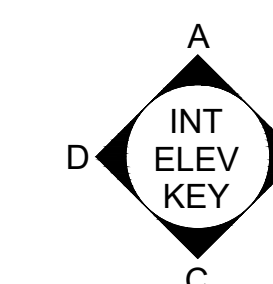

PLAN
NORTH




SCALE: 1 : 100

ALL DIMENSIONS AND/OR DIMENSIONS SHOWN IN
CALLOUT/ NOTES ARE IN MILLIMETERS UNLESS
OTHERWISE NOTED.

A1 OS - TELECOM PLAN (CLIN 0002)

1:100

P —
 O —
 N —
 M —
 L —
 K —
 J —
 I —
 H —
 G —
 F —
 E —
 D —
 C —
 B —
 A

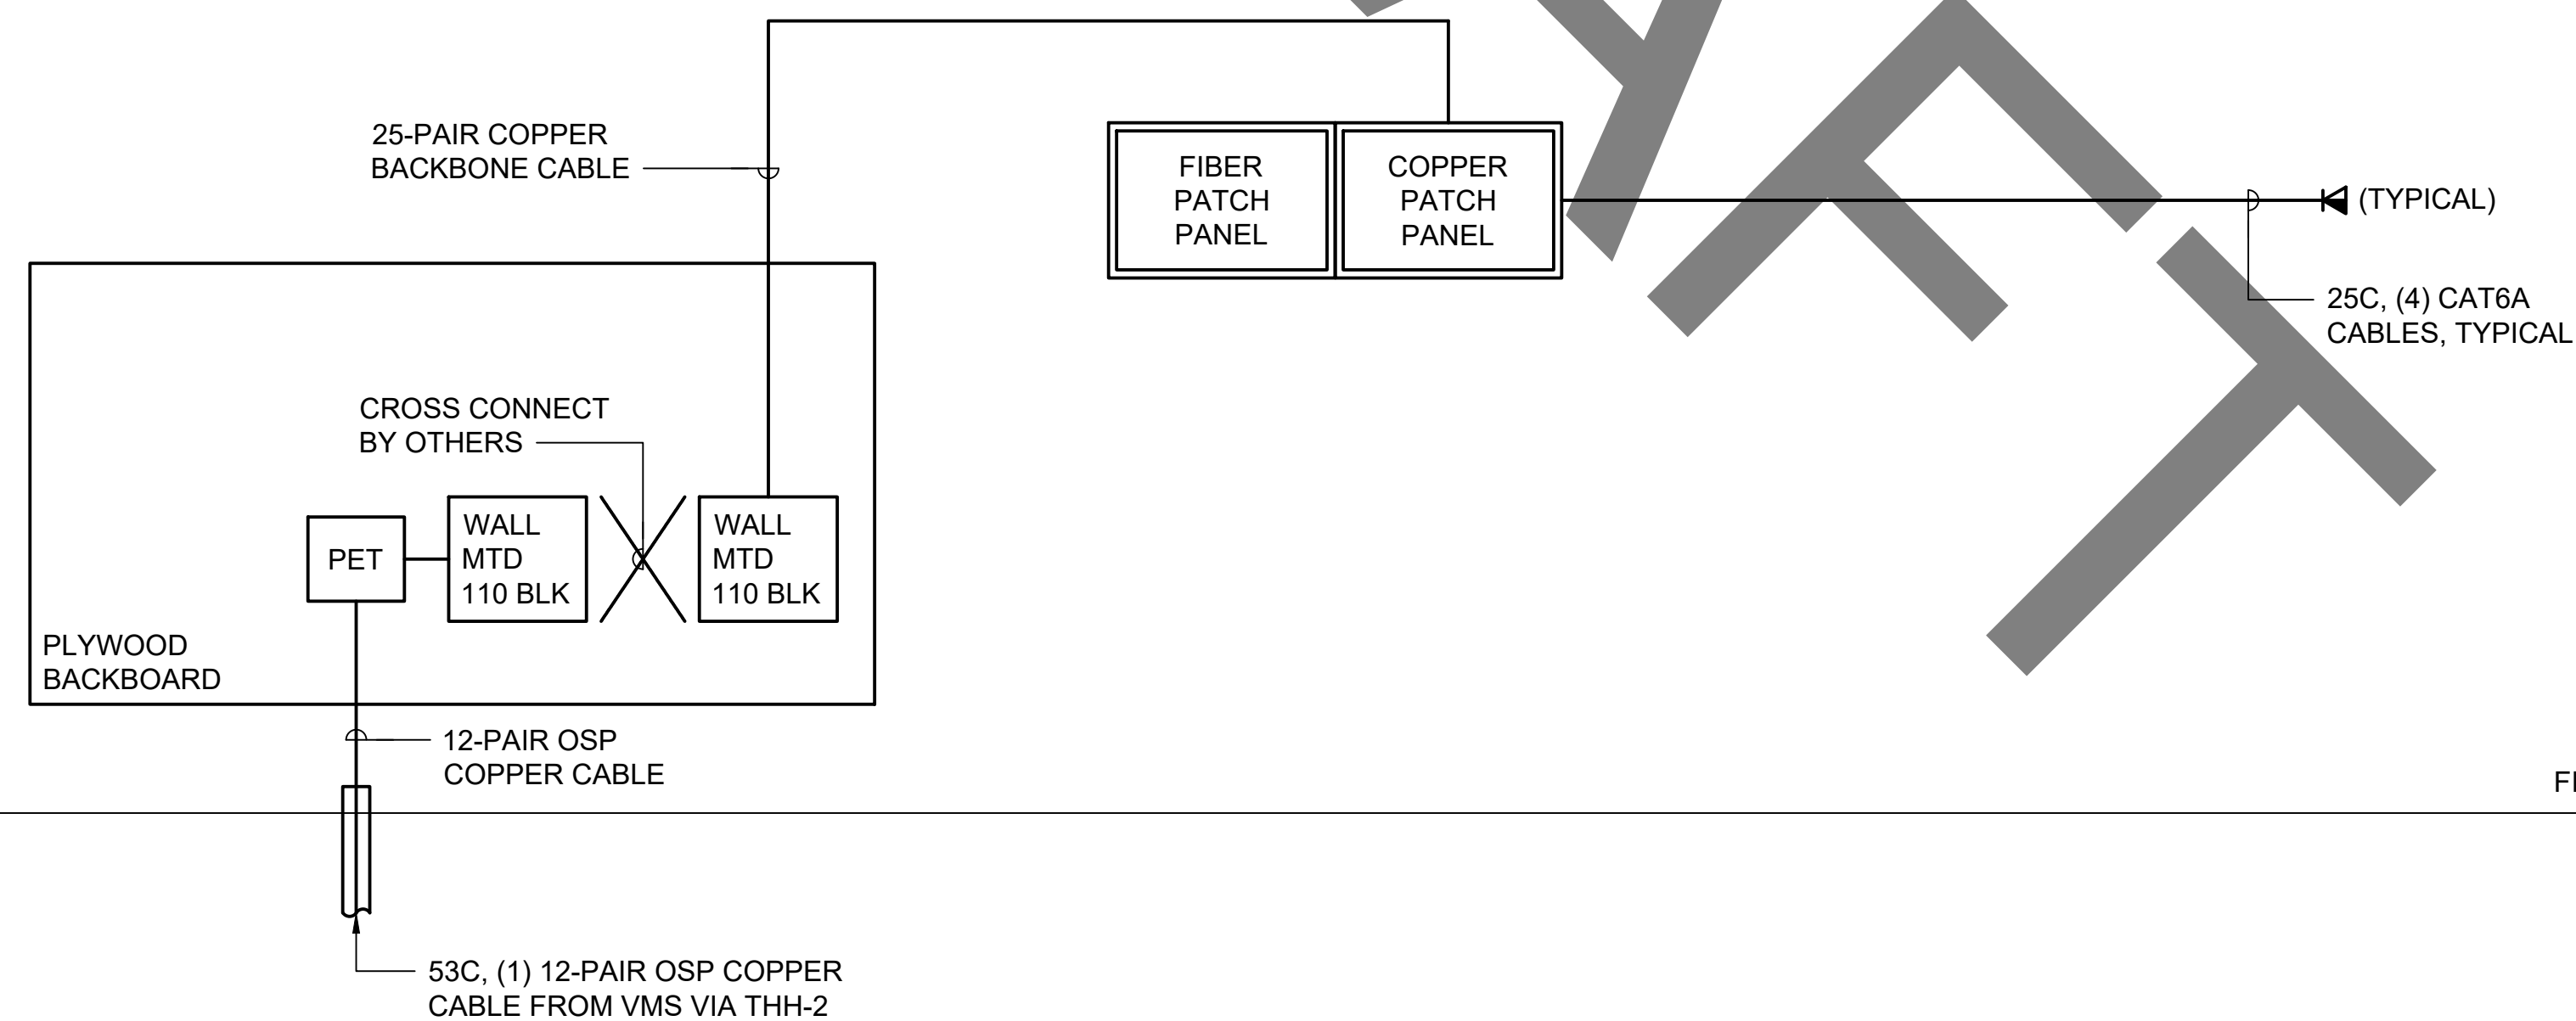

FIRST FLOOR

CLIN 0002



US Army Corps
of Engineers®

[illegible]

US ARMY CORPS OF ENGINEERS JAPAN DISTRICT, OKINAWA AREA OFFICE 501 SUMNER STREET, WHITE 620 FORT BELVOIR, HAWAII 96317	SSM INTERNATIONAL, INC. 501 SUMNER STREET, WHITE 620 FORT BELVOIR, HAWAII 96317		DESIGNED BY: U.S. ARMY JPO AP-96374-5102	SOLICITATION NO.: 96374-5102	SCALE: AS SHOWN
			DRAWN BY: U.S. ARMY JPO AP-96374-5102	CHECKED BY: U.S. ARMY JPO AP-96374-5102	CONTRACT NO.: 96374-5102
			SUBMITTED BY: U.S. ARMY JPO AP-96374-5102	FILE NAME: ISO A1	

OS - TELECOM RISER DIAGRAM (CLIN 0002)

SHEET ID



TB601

INTERMEDIATE DESIGN




SHEET ID
TD101

INTERMEDIATE DESIGN

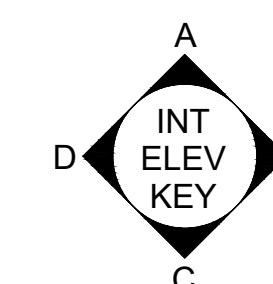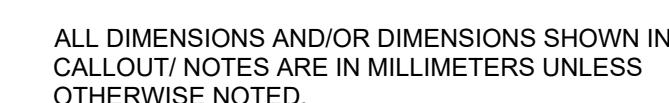

GENERAL NOTES

US Army Corps
of Engineers®[illegible]

 US ARMY CORPS OF ENGINEERS JAPAN DISTRICT, OKINAWA AREA OFFICE USED-J UNIT 35132 APO, AP 96374-5132	DESIGNED BY: DRAWN BY: CHECKED BY: SUBMITTED BY: FILE NAME:	ISSUE DATE: SOLICITATION NO.: CONTRACT NO.: SCALE: AS SHOWN
	SSFM INTERNATIONAL, INC 501 SUMMER STREET, SUITE 620	


KADENA AIR BASE, OKINAWA, JAPAN
VEHICLE MAINTENANCE SHOP
FY20 MCA PNT77833

SAW - PARTIAL TELECOM PLAN - ZONE A (CLIN 0004)

SHEET ID


TD111

INTERMEDIATE DESIGN

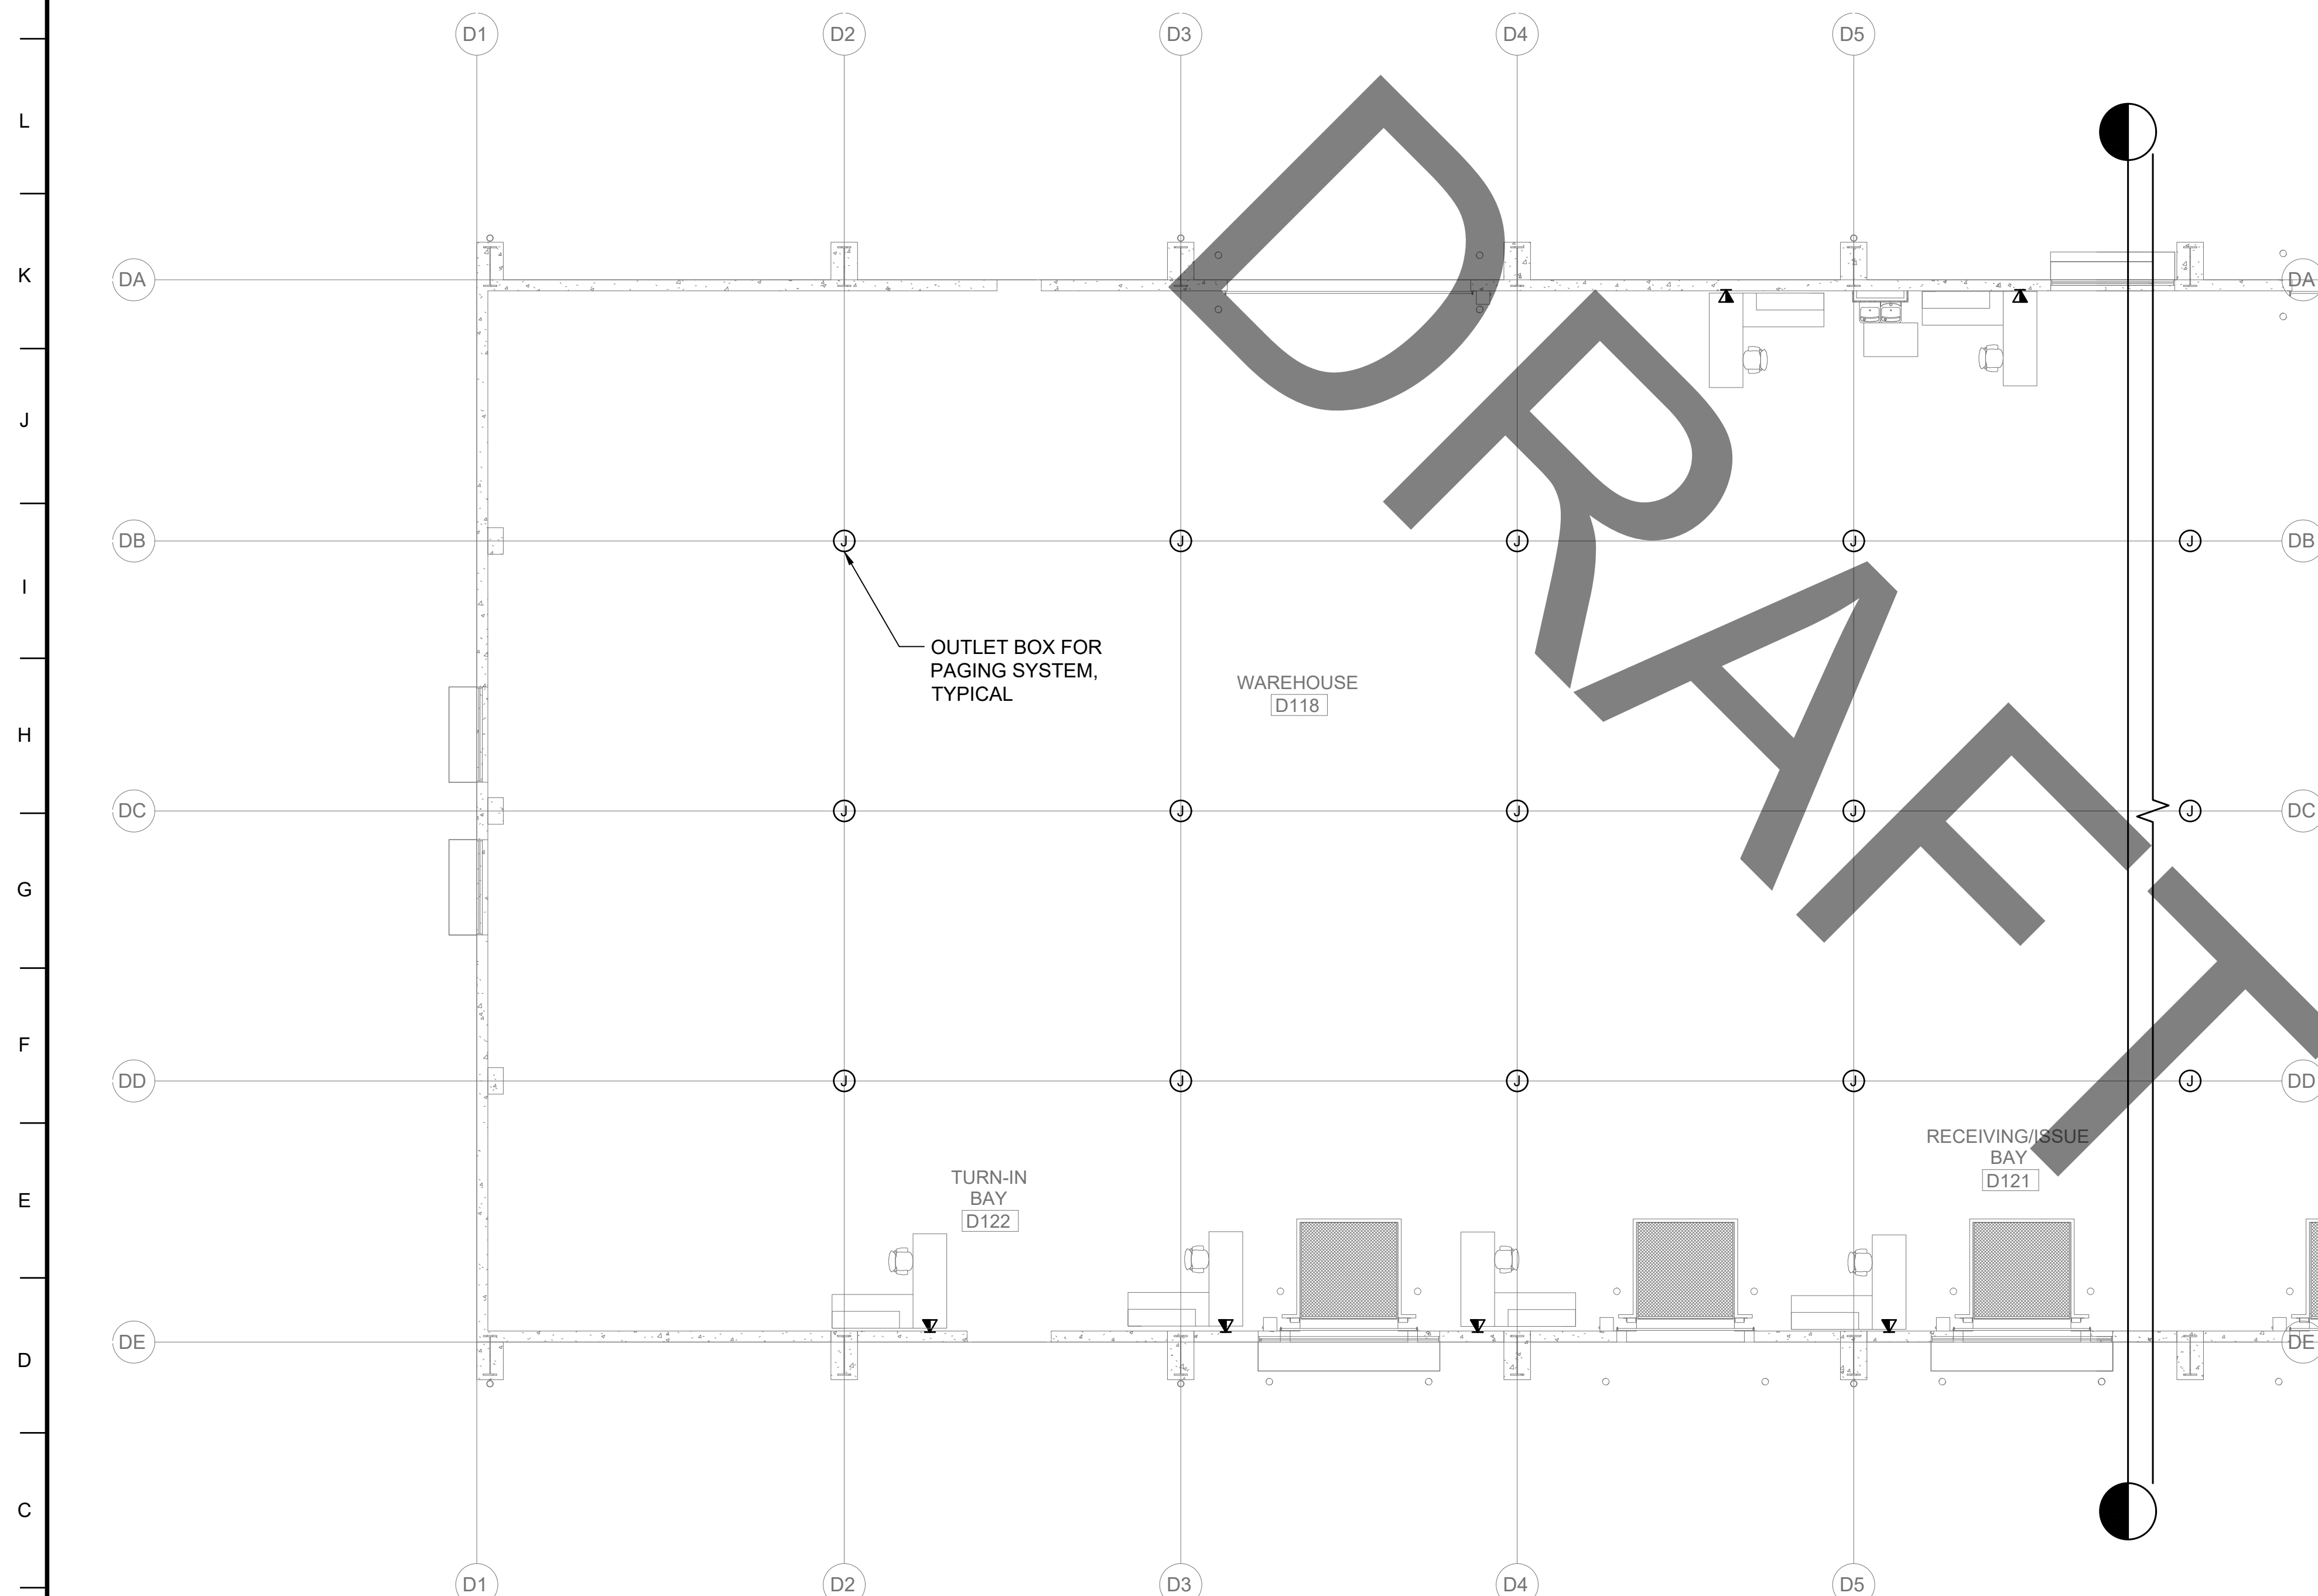


CLIN 0004

KEY PLAN

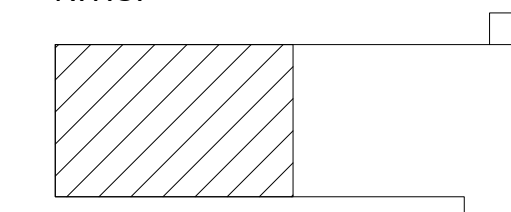SSAW
N.T.S.


GRAPHIC SCALE

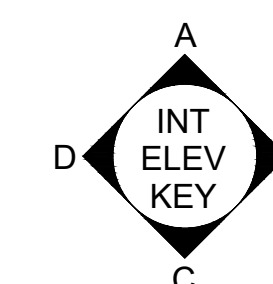

PLAN
NORTH



SCALE: 1 : 100

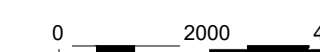


ALL DIMENSIONS AND/OR DIMENSIONS SHOWN IN
CALLOUT/ NOTES ARE IN MILLIMETERS UNLESS
OTHERWISE NOTED.


SSAW - PARTIAL TELECOM PLAN - ZONE A (CLIN 0004)

1.10

— P
— O
— N
— M
— L
— K
— J
— I
— H
— G
— F
— E
— D
— C
— B
— A

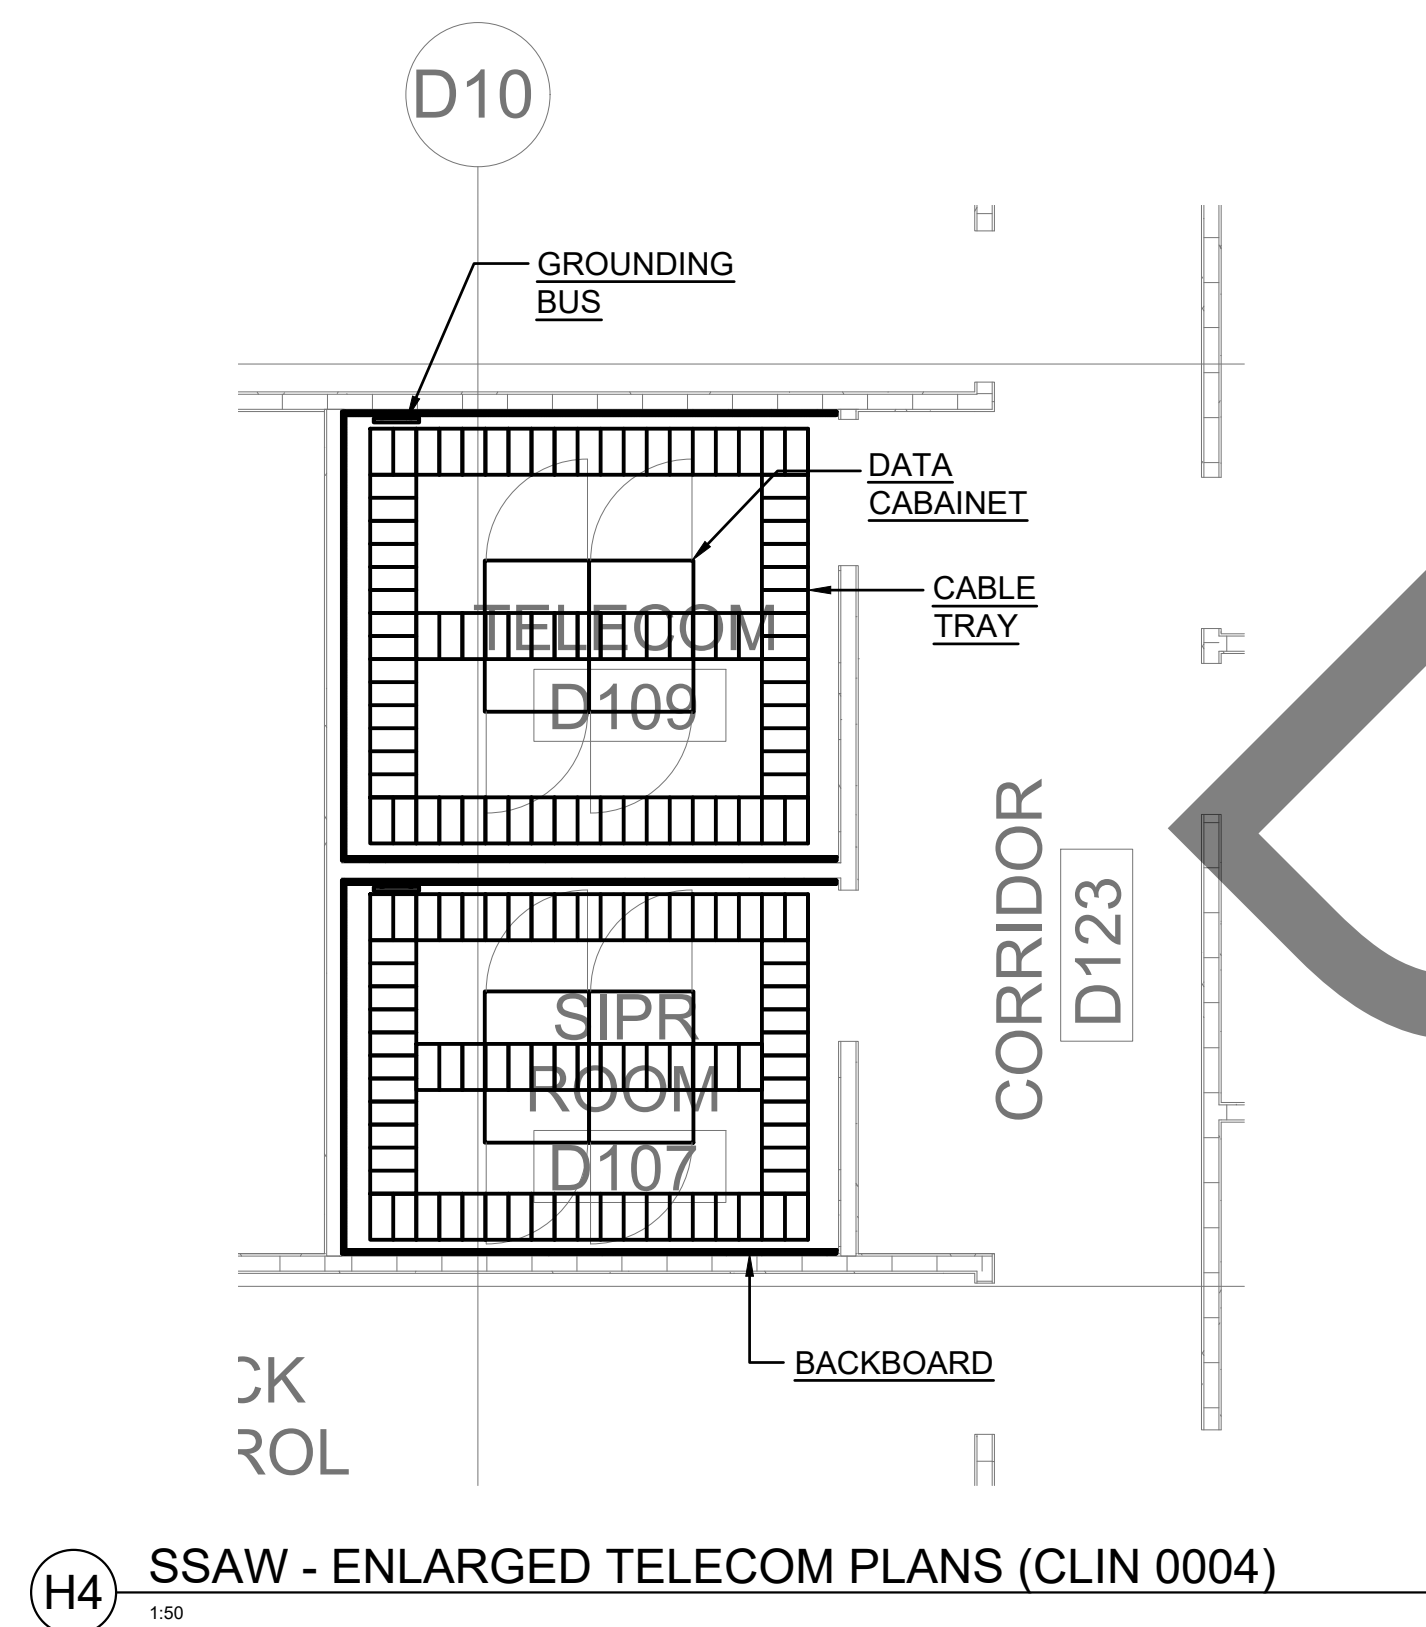

GENERAL NOTES

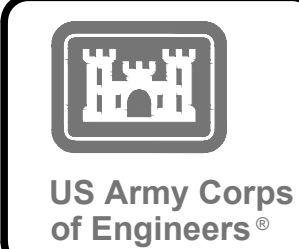[illegible]

US ARMY CORPS OF ENGINEERS JAPAN DISTRICT, OKINAWA AREA OFFICE USASD-J, UNIT 35132 APO, AP 96374-5132		DESIGNED BY: DRAWN BY: CHECKED BY: SUBMITTED BY: SCALE: AS SHOWN		ISSUE DATE: SOLICITATION NO.: CONTRACT NO.: FILE NAME: 501 SUMNER STREET, SUITE 620 11	
		SSPM INTERNATIONAL, INC. 501 SUMNER STREET, SUITE 620			

KADENA AIR BASE, OKINAWA, JAPAN
VEHICLE MAINTENANCE SHOP
FY20 MCA PN77833

SHEET ID

TD401

INTERMEDIATE DESIGN

LEGEND

CLIN 0004

GRAPHIC SCALE



SCALE: 1 : 50



ALL DIMENSIONS AND/OR DIMENSIONS SHOWN IN
CALLOUT/ NOTES ARE IN MILLIMETERS UNLESS
OTHERWISE NOTED.

[illegible]


JAPAN DISTRICT, OKINAWA AREA OFFICE USED-1, UNIT 35132 APO, AP 96374-5132		 SSFM INTERNATIONAL, INC 501 SUMMER STREET, SUITE 620	SOLICITATION NO.: CONTRACT NO.: SCALE: AS SHOWN FILE NAME: SIZE:
DRAWN BY:	CHECKED BY:	SUBMITTED BY:	

SSAW - TELECOM RISER DIAGRAM (CLIN 0004)

SHEET ID

TD601


INTERMEDIATE DESIGN

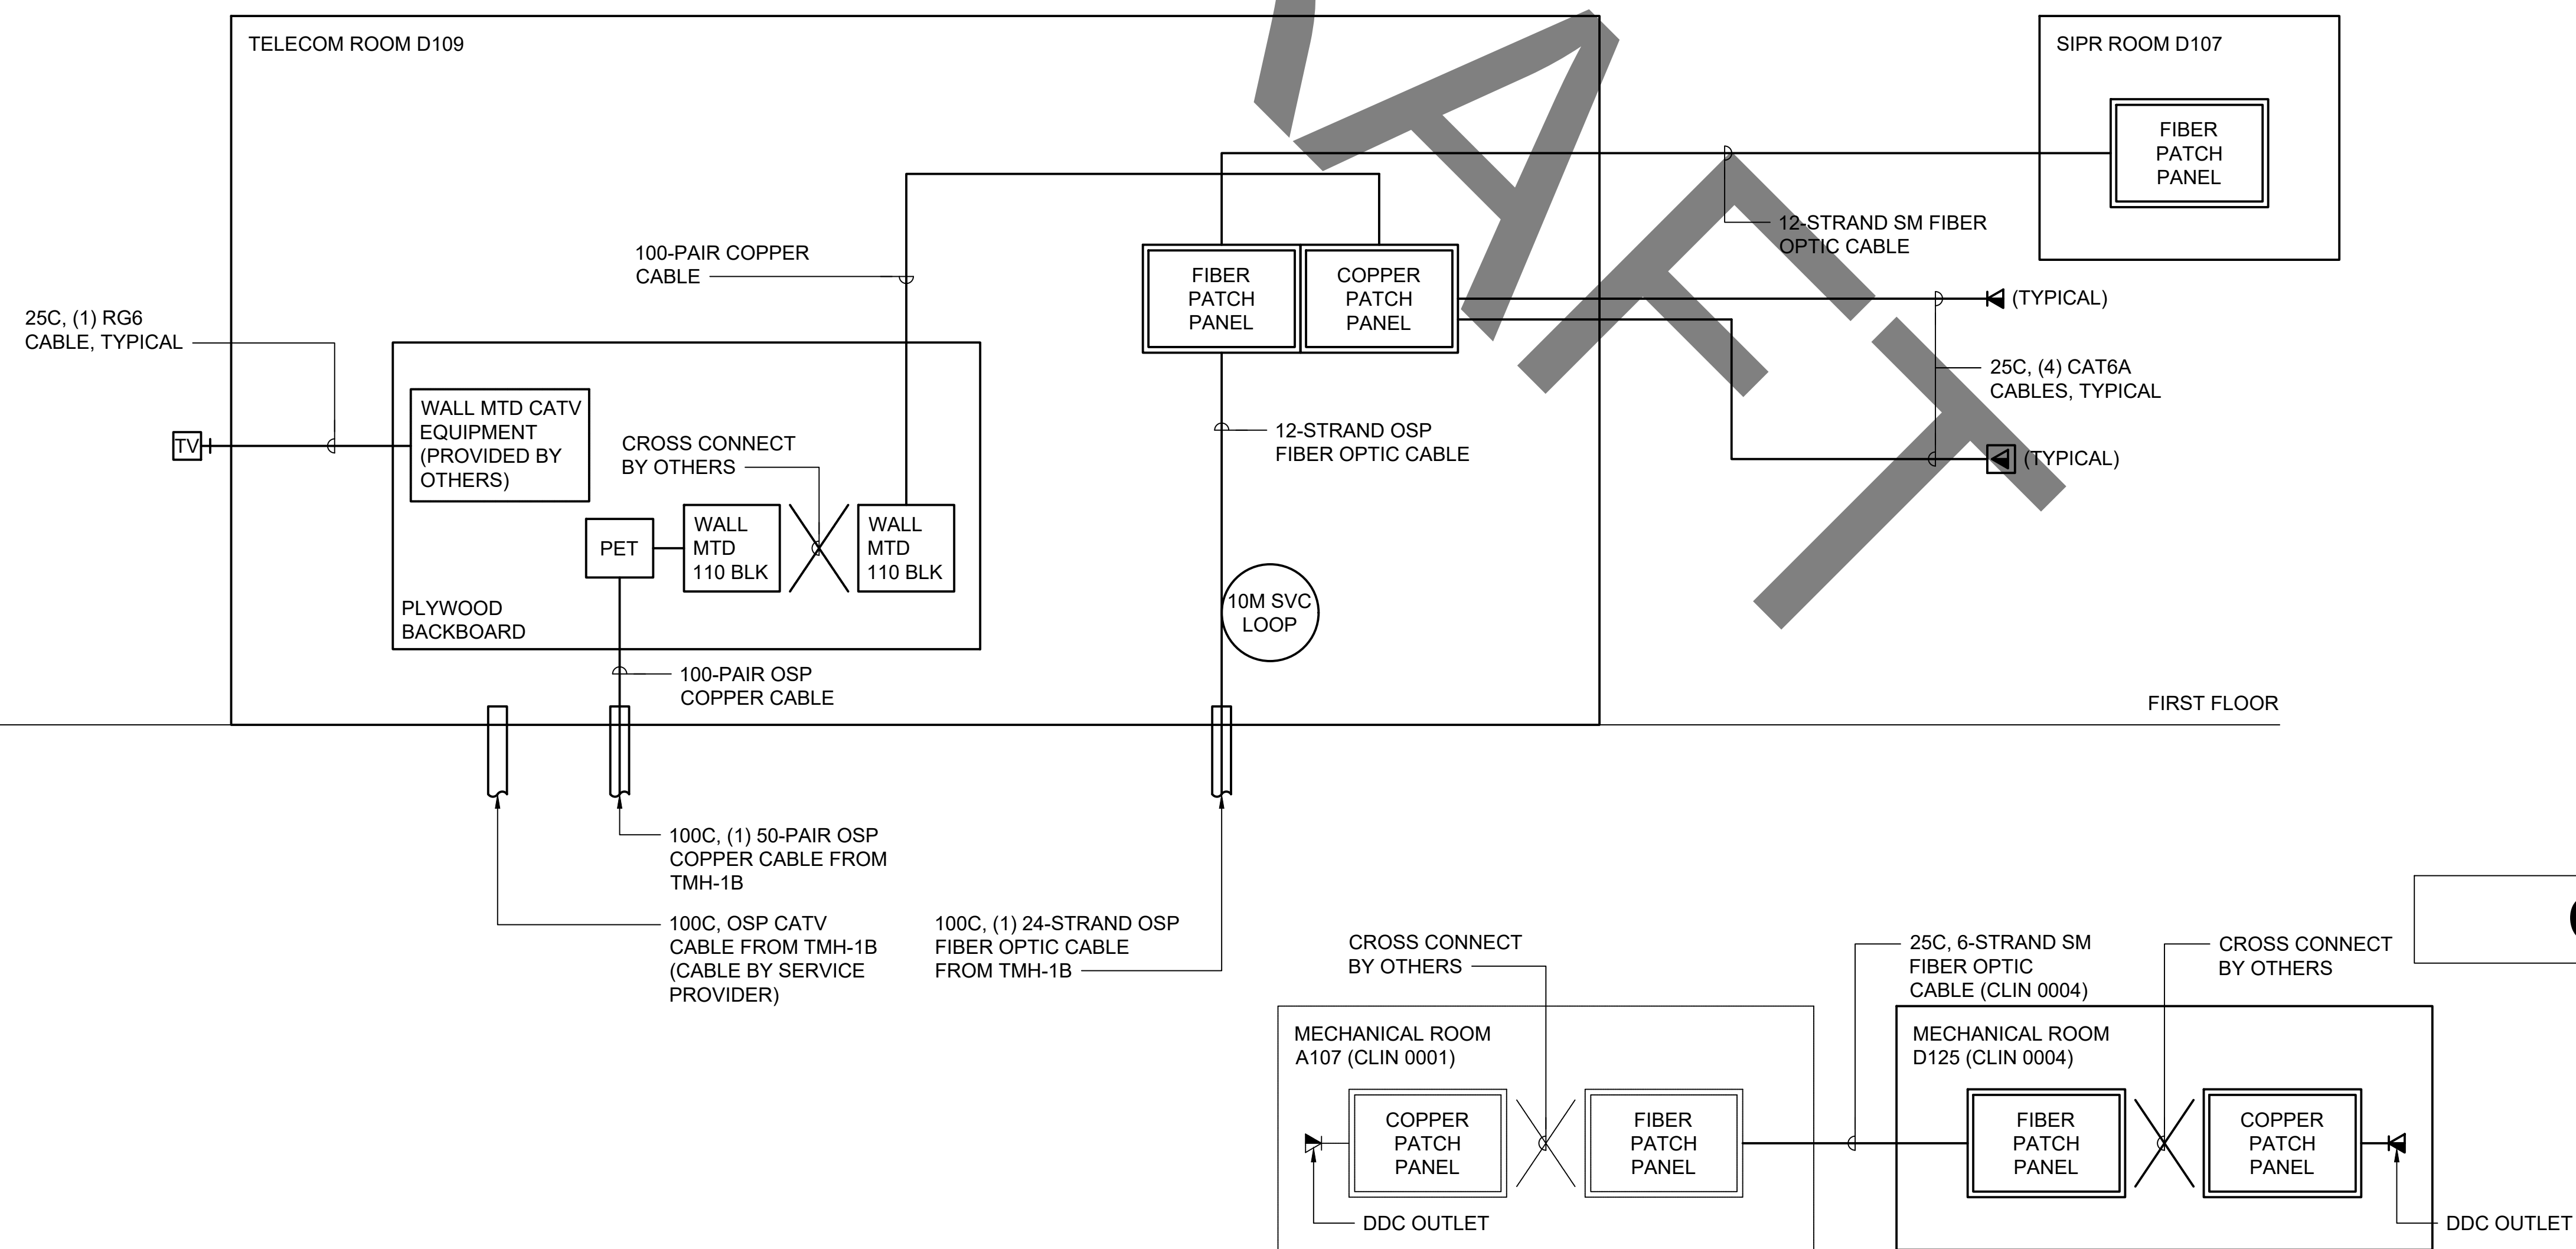


CLIN 0004

A1 **SSAW - TELECOM RISER DIAGRAM (CLIN 0004)**
NO SCALE

NO SCALE

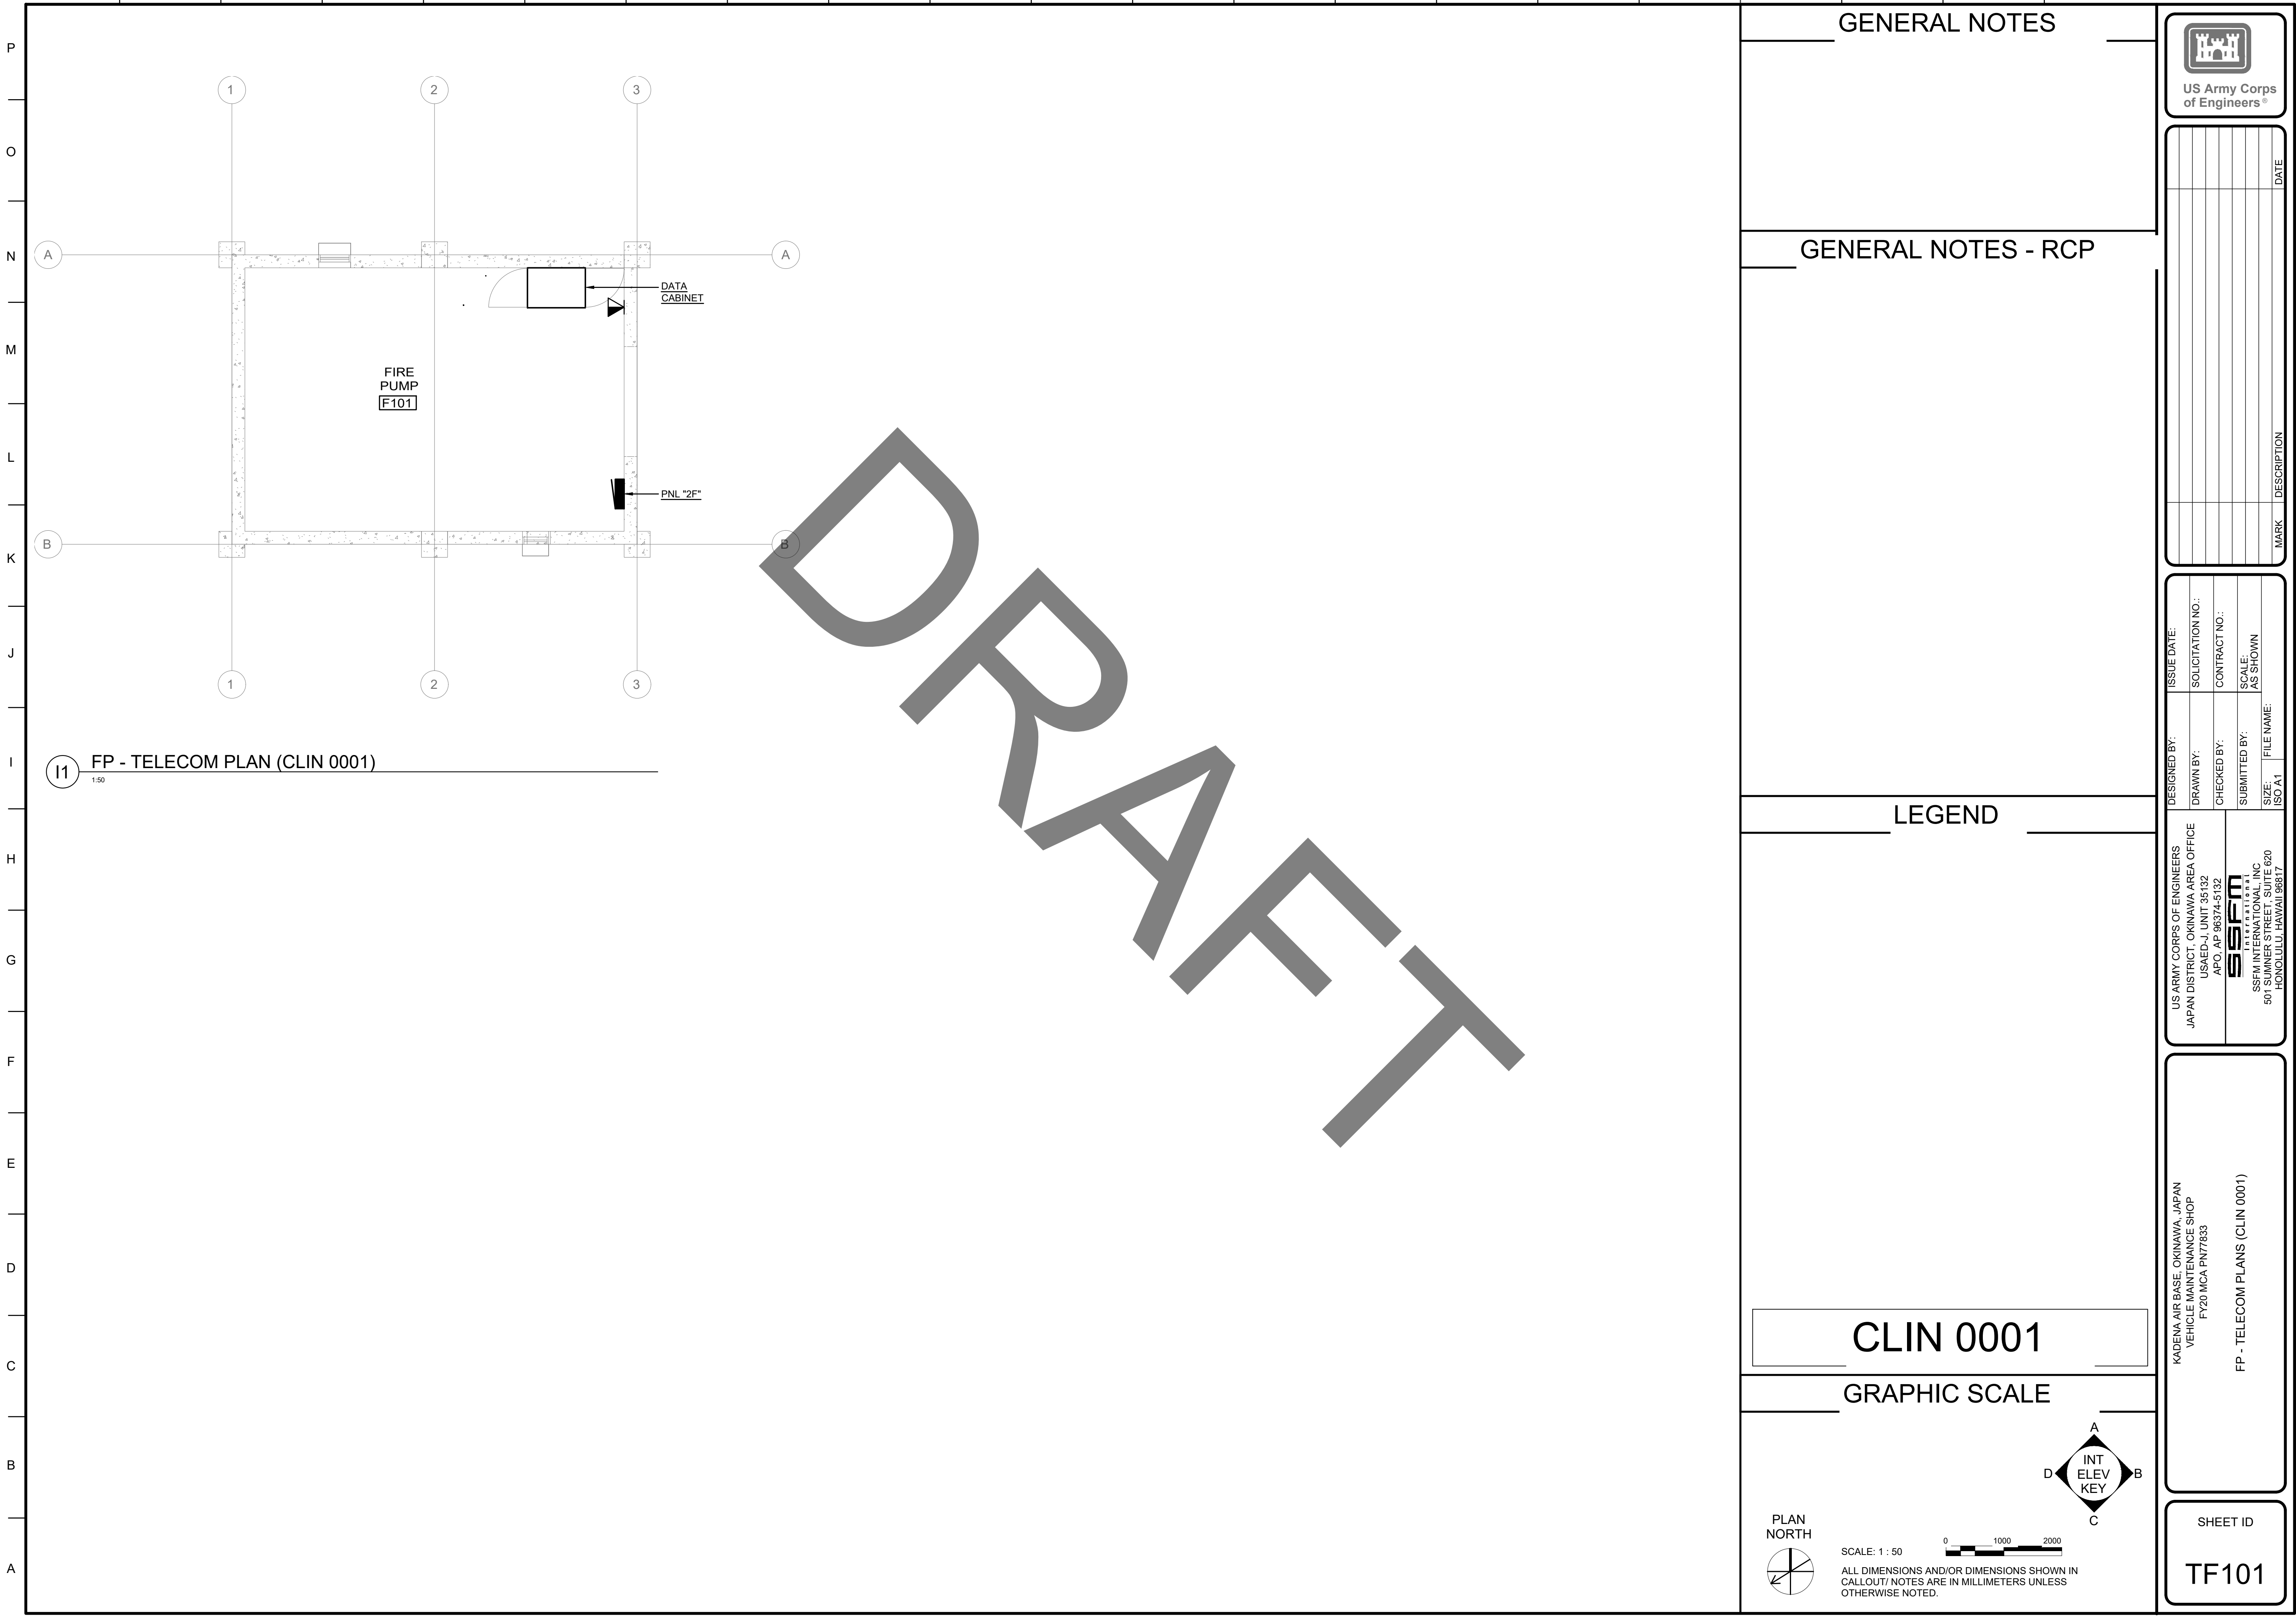

P
 —
 O
 —
 N
 —
 M
 —
 L
 —
 K
 —
 J
 —
 I
 —
 H
 —
 G
 —
 F
 —
 E
 —
 D
 —
 C
 —
 B
 —
 A

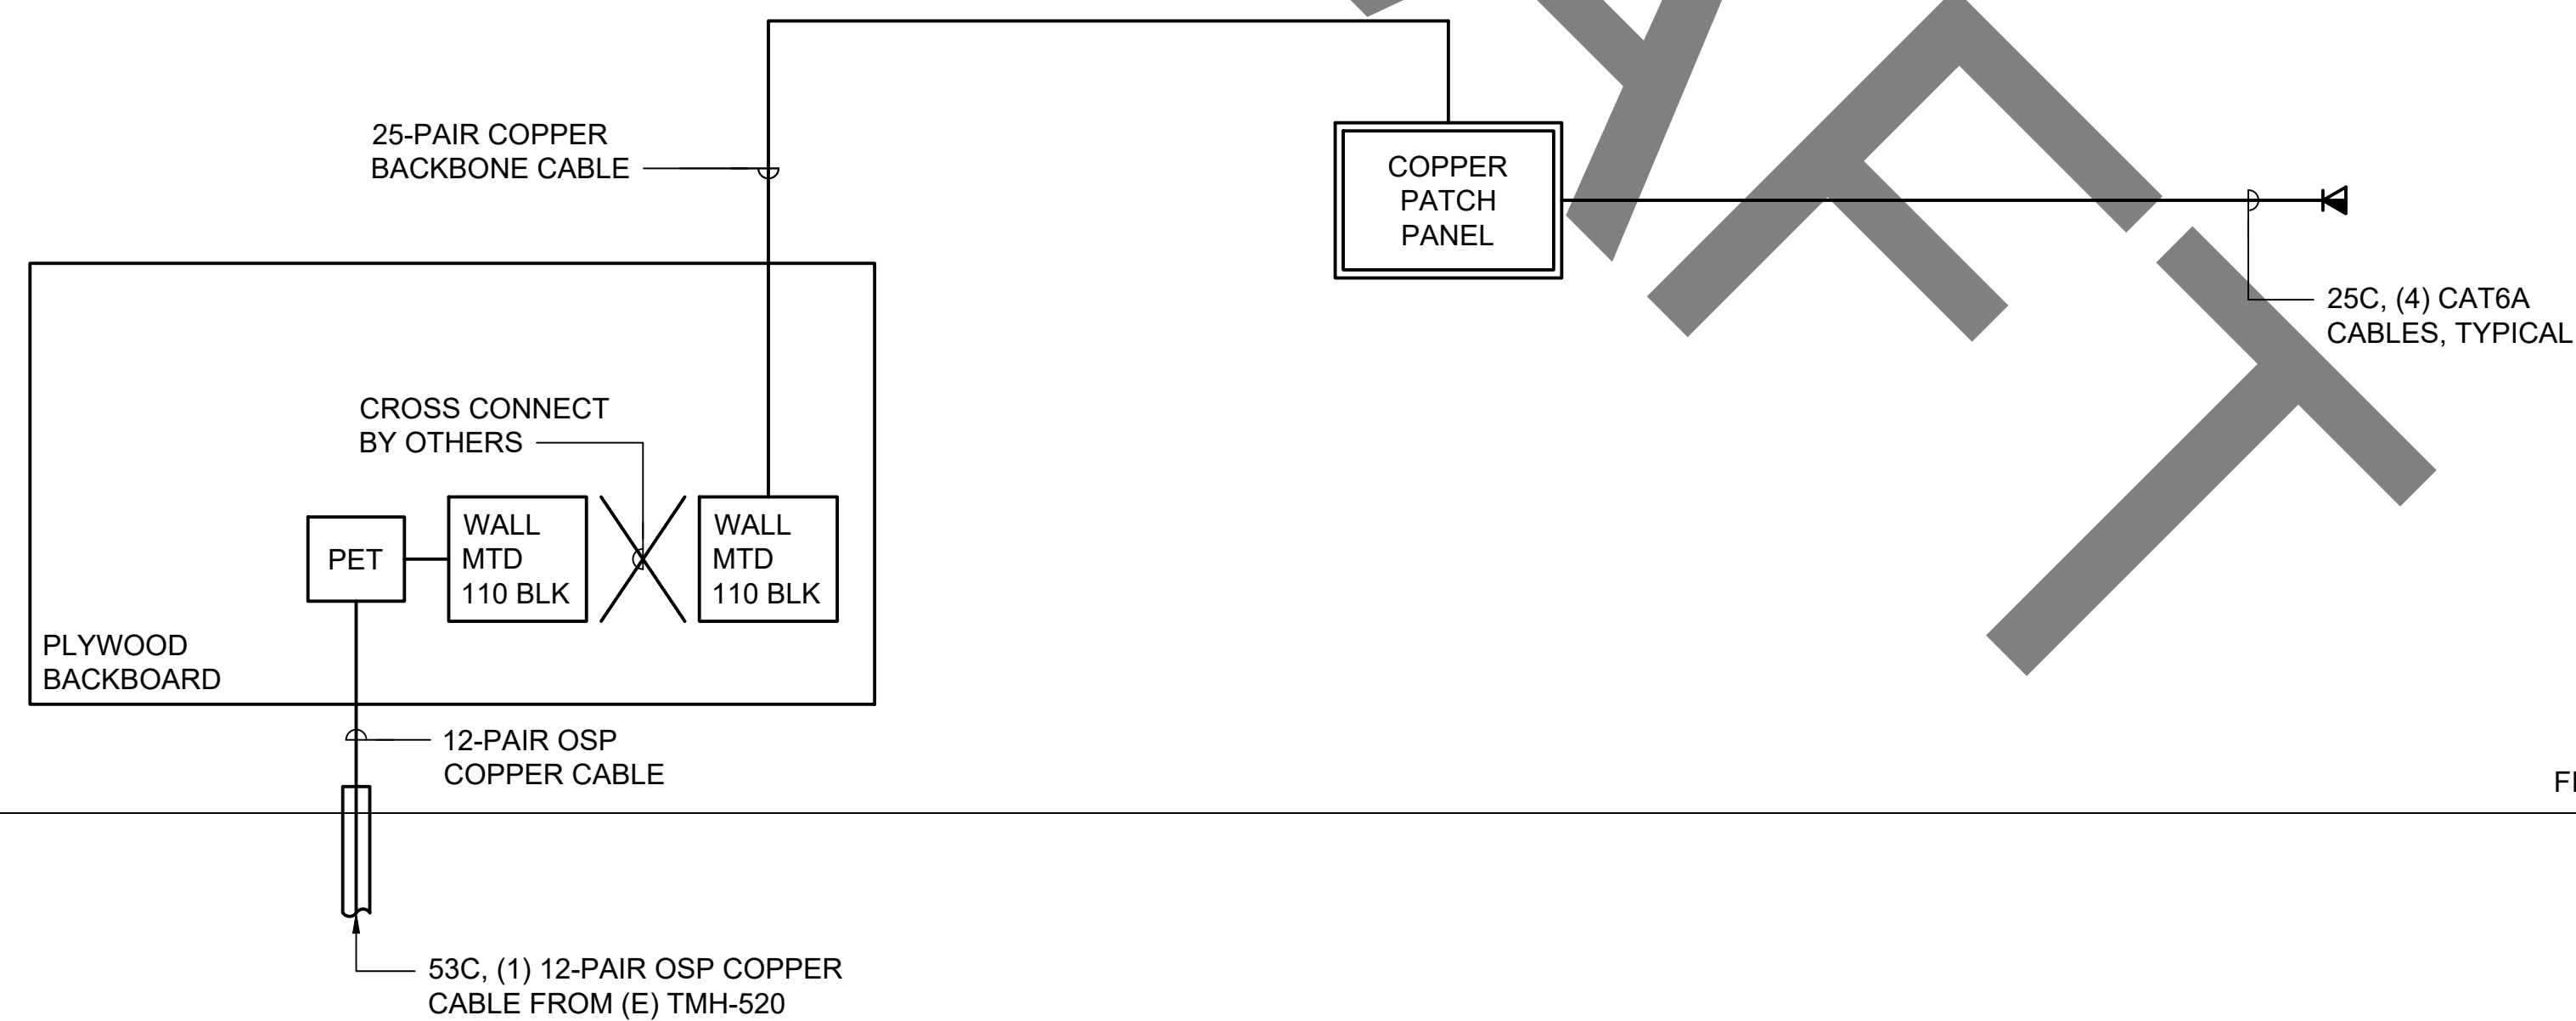

FIRST FLOOR

CLIN 0001

US Army Corps
of Engineers®[illegible]

SSM INTERNATIONAL, INC. 501 SUMMER STREET, SUITE 620 JAPAN DISTRICT, OKINAWA AREA OFFICE US ARMY CORPS OF ENGINEERS USASD-J UNIT 35132 APO, AP 96374-5132	DESIGNED BY:	ISSUE DATE:
	DRAWN BY:	SOLUTION NO.:
	CHECKED BY:	CONTRACT NO.:
	SUBMITTED BY:	SCALE:
	SIZE:	FILE NAME:
		AS SHOWN

KADENA AIR BASE, OKINAWA, JAPAN
VEHICLE MAINTENANCE SHOP
FY20 MCA PN77833

FP - TELECOM RISER DIAGRAM (CLIN 0001)


SHEET ID

TF601

INTERMEDIATE DESIGN

FP - TELECOM RISER DIAGRAM (CLIN 0001)

NO SCALE

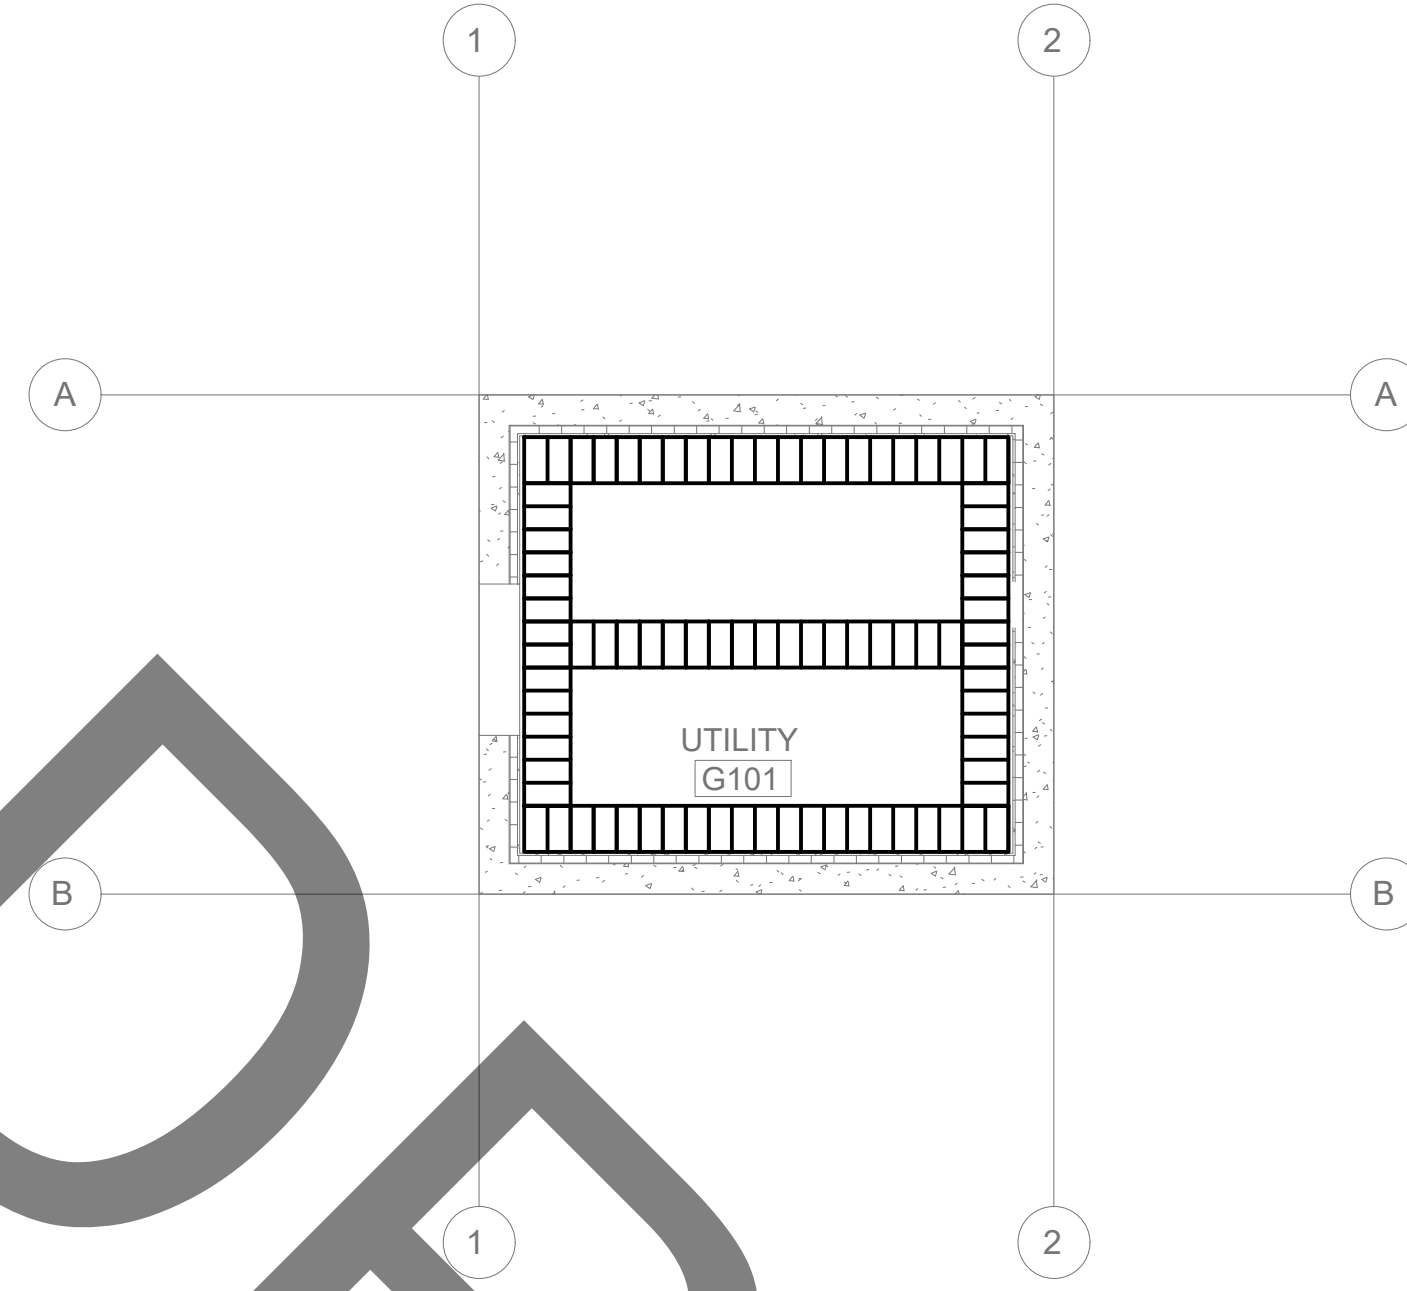

19 CH - REFLECTED CEILING PLAN (CLIN 0001)

GENERAL NOTES - RCP

[illegible]


DESIGNED BY:	ISSUE DATE:
US ARMY CORPS OF ENGINEERS	
JAPAN DISTRICT, OKINAWA AREA OFFICE	
DRAWN BY:	SOLICITATION NO.:
UNIT 35132	
ATD-JA 9537-4-032	
	
SSFM INTERNATIONAL, INC	
501 SUMNER STREET, SUITE 620	
HONOLULU, HAWAII 96817	
CHECKED BY:	CONTRACT NO.:
SUBMITTED BY:	SCALE:
	AS SHOWN
SIZE:	FILE NAME:
ISO A1	

CH - IELECOM PLANS (CLIN 0001)

TG101


INTERMEDIATE DESIGN

CLIN 0001

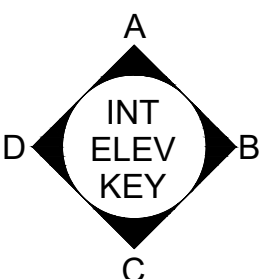

ALL DIMENSIONS AND/OR DIMENSIONS SHOWN IN
CALLOUT/ NOTES ARE IN MILLIMETERS UNLESS
OTHERWISE NOTED.

A

 

1. SEE TS611 AND TS621 FOR OUTSIDE PLANT CABLE ASSIGNMENT.

(A1)


NO SCALE

TG601

INTERMEDIATE DESIGN

19 COF SS - ENLARGED 2ND FLOOR TELECOM ROOM

1:50

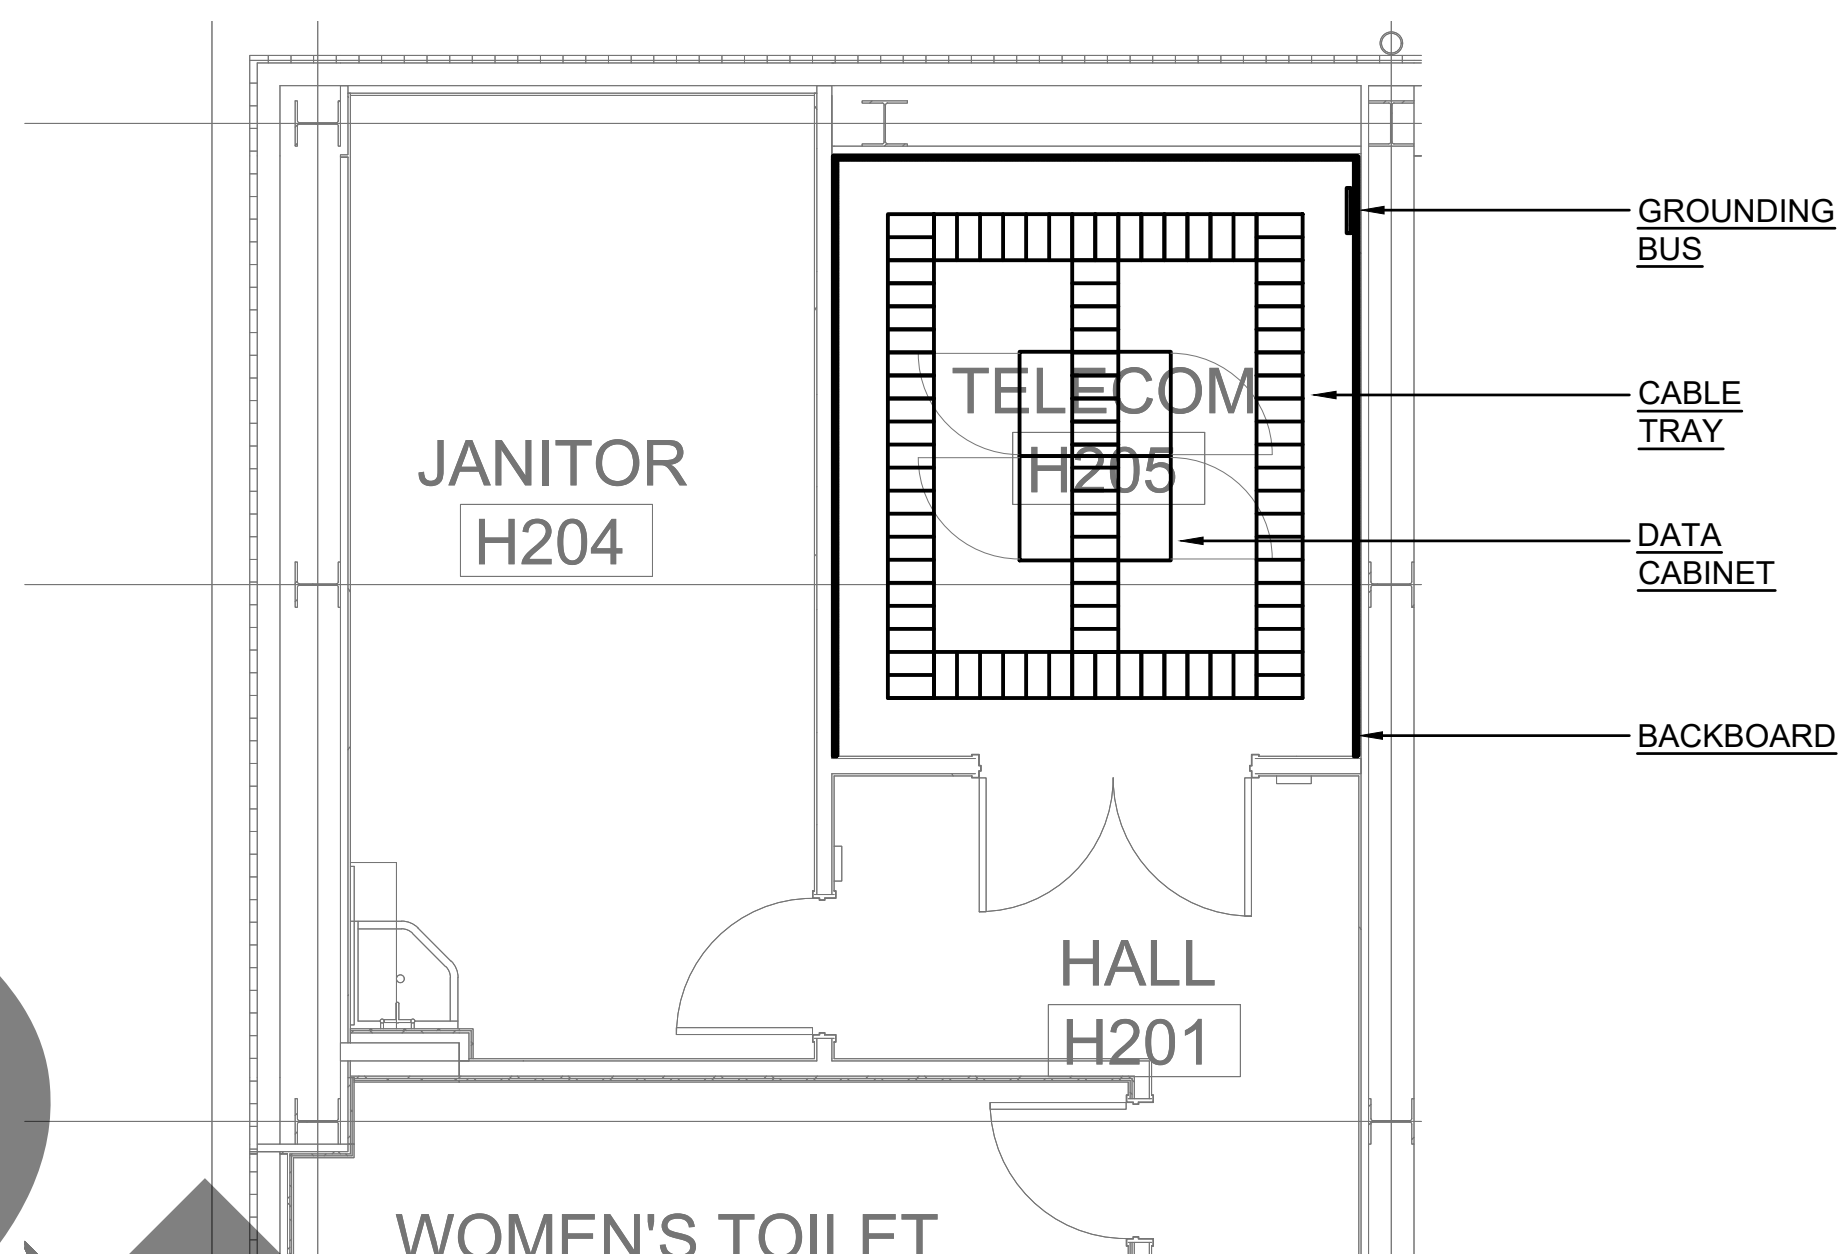

19 COF SS - ENLARGED 2ND FLOOR TELECOM ROOM
1:50

GENERAL NOTES

[illegible]

US ARMY CORPS OF ENGINEERS JAPAN DISTRICT, OKINAWA AREA OFFICE USAED-4 UNIT 35132 APO AP 96374-5132	DESIGNED BY:	ISSUE DATE:
	DRAWN BY:	SOLICITATION NO.:
	CHECKED BY:	CONTRACT NO.:
	SUBMITTED BY:	SCALE:
	SIZE:	FILE NAME:

KADENA AIR BASE, OKINAWA, JAPAN
VEHICLE MAINTENANCE SHOP
FY20 MCA PN77833

SHEET ID

TH40


INTERMEDIATE DESIGN

CLIN 0004


GRAPHIC SCALE



SCALE: 1 : 50

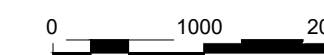

ALL DIMENSIONS AND/OR DIMENSIONS SHOWN IN
CALLOUT/ NOTES ARE IN MILLIMETERS UNLESS
OTHERWISE NOTED.

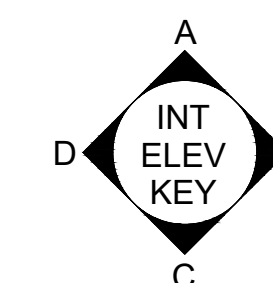

[illegible]


JAPAN DISTRICT, OKINAWA AREA OFFICE USAED-J UNIT 35132 APO, AP 96374-5132	DRAWN BY:	SOLICITATION NO.:
	CHECKED BY:	CONTRACT NO.:
	SUBMITTED BY:	SCALE: AS SHOWN
	SIZE:	FILE NAME:

COF SS - TELECOM RISER DIAGRAM (CLIN 0004)


SHEET ID

TH60

INTERMEDIATE DESIGN

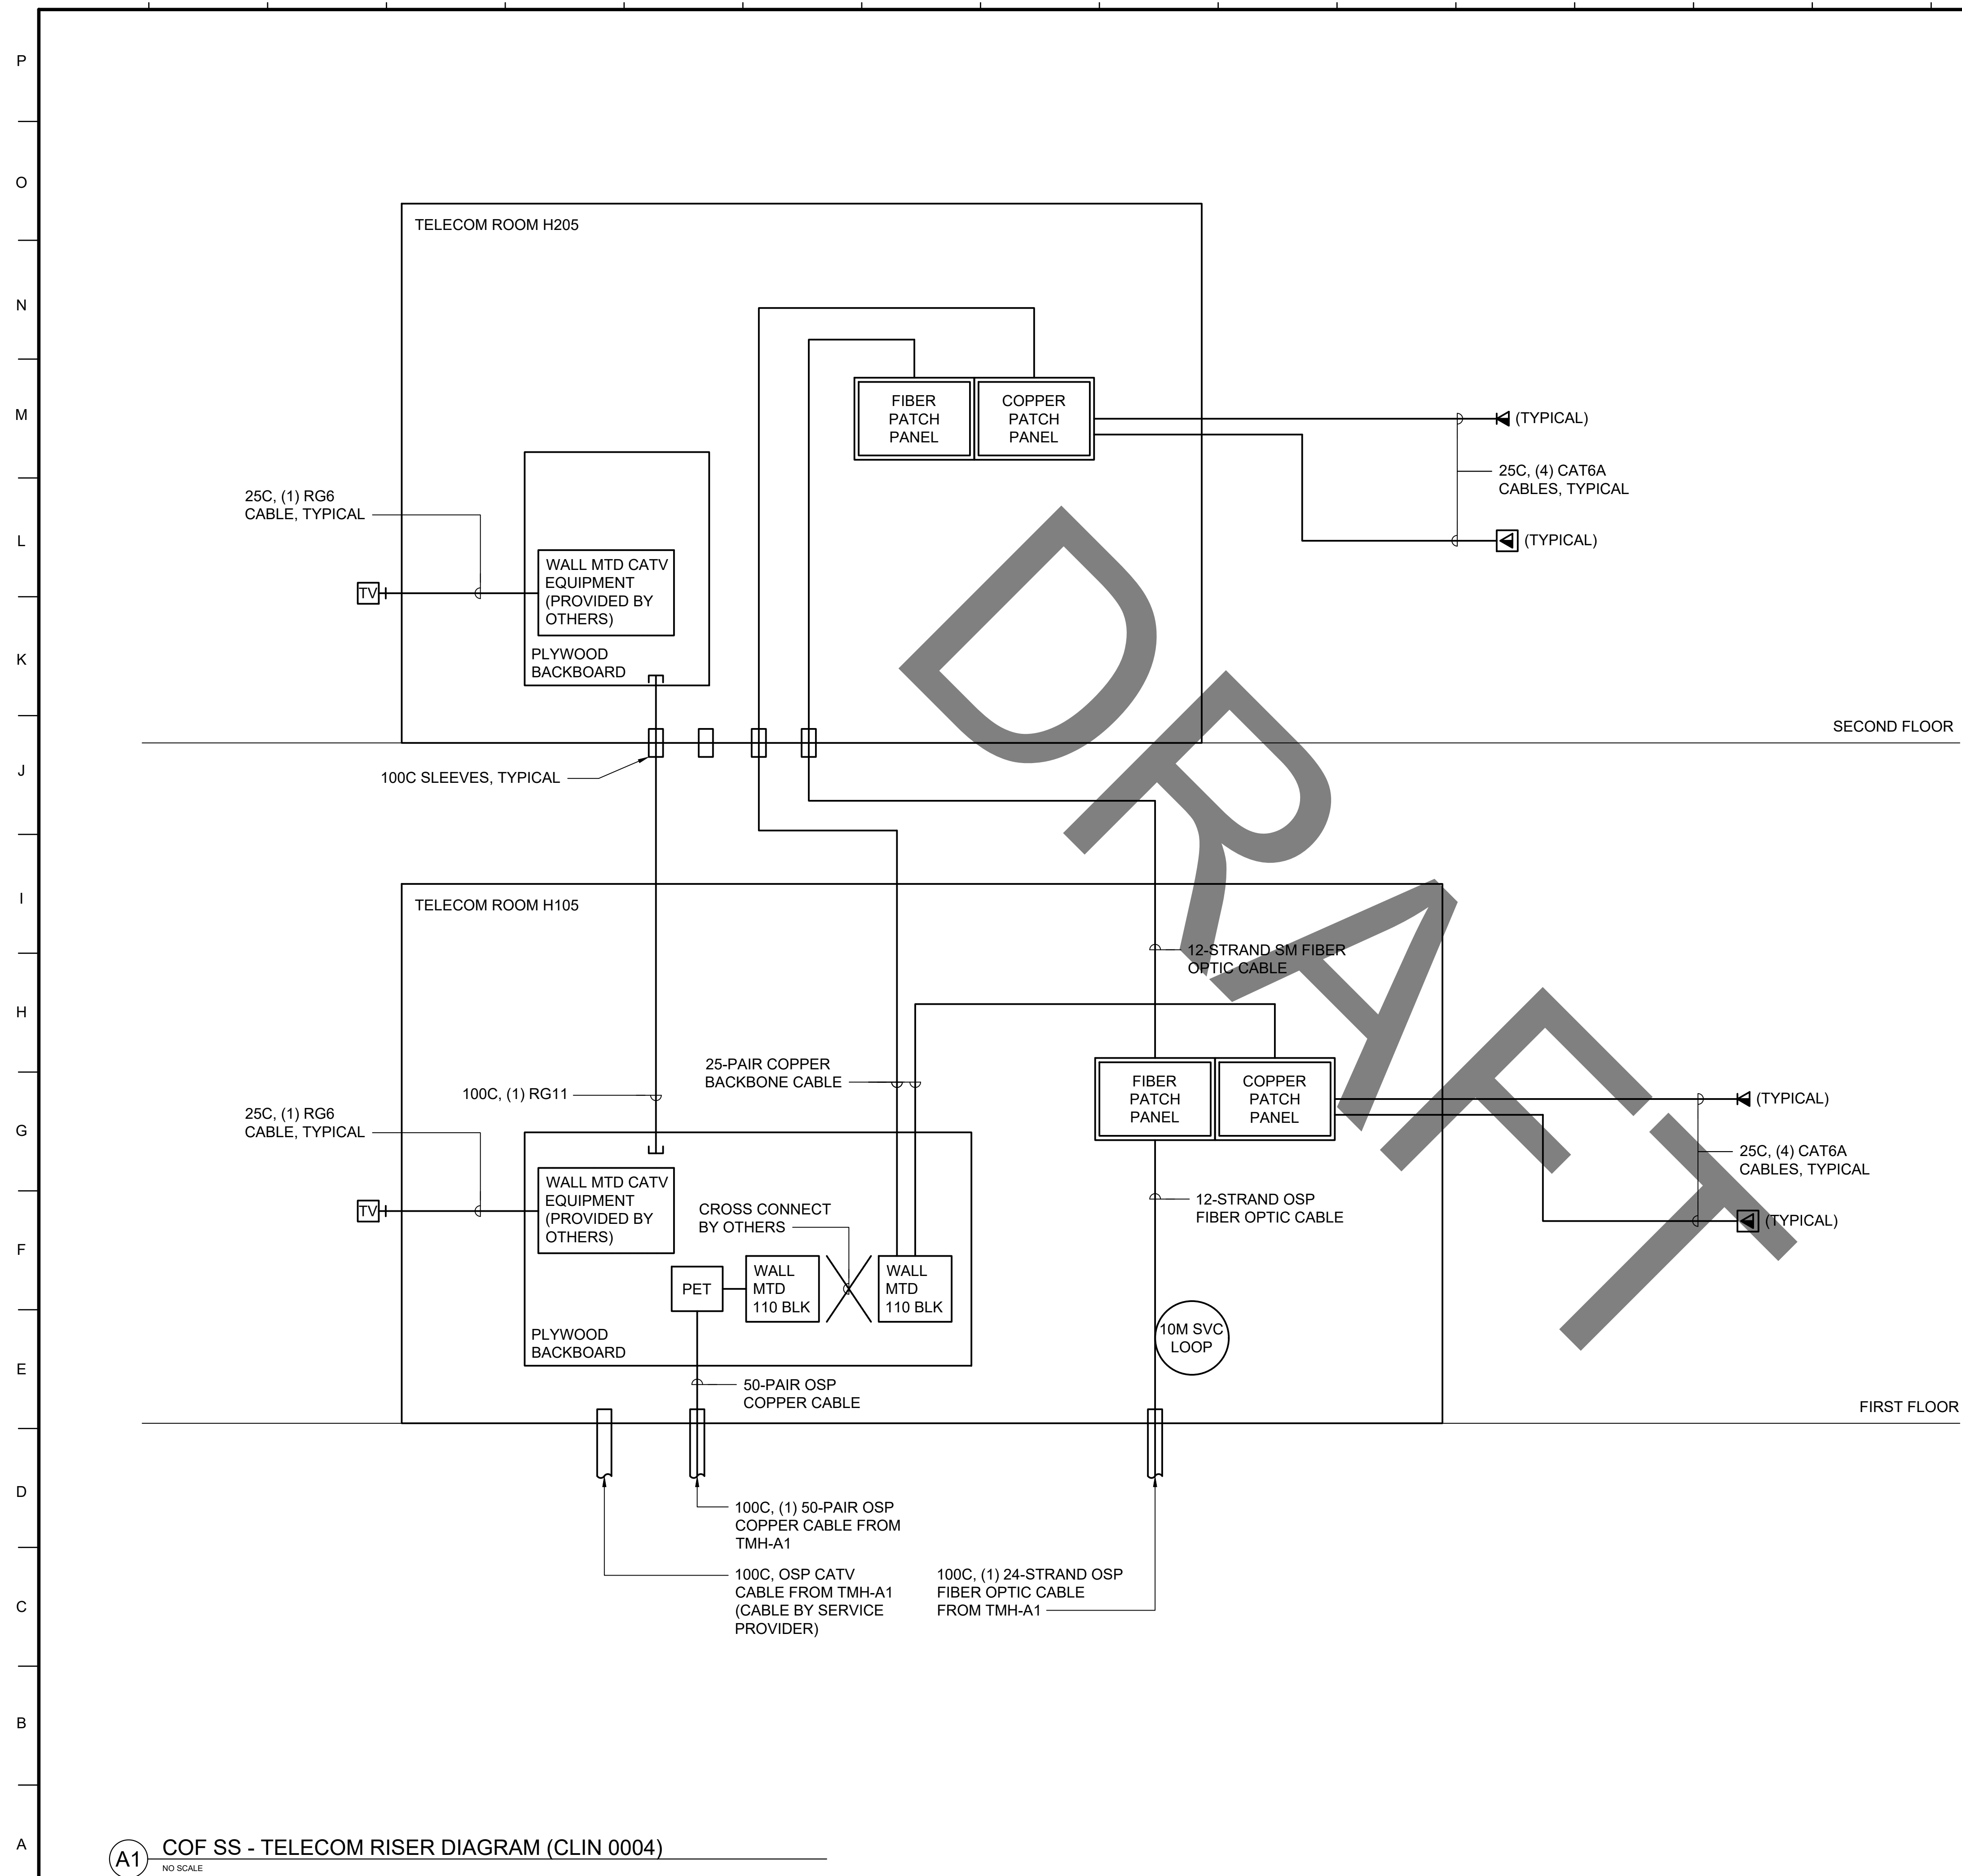


A — B — C — D — E — F — G — H — I — J — K — L — M — N — O — P

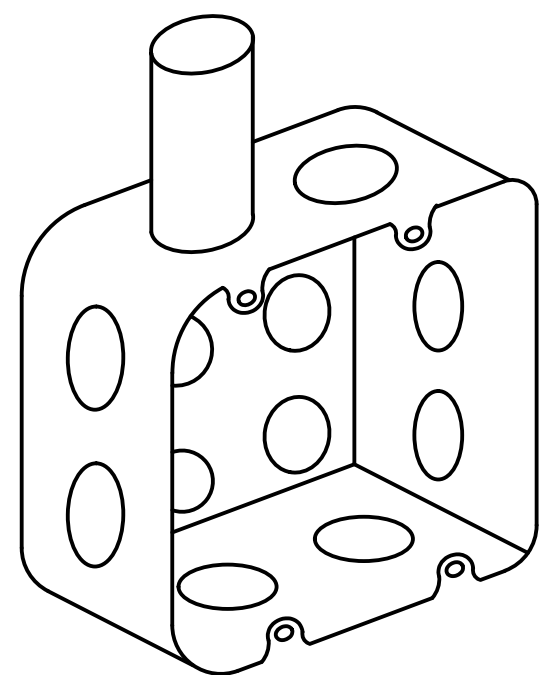


100mm SQUARE X 66mm DEEP
20mm AND 25mm KNOCKOUTS

FOR CATV, WIRELESS ACCESS
POINTS, CCTV, ALL INTERCOM
AND PAGING DEVICES

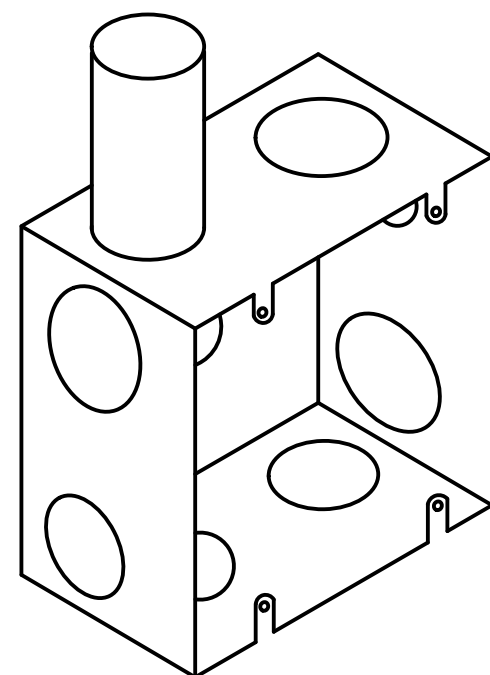


125mm SQUARE X 75mm DEEP
25mm AND 30mm KNOCKOUTS

FOR ALL WALL OR COLUMN
MOUNTED DATA/TEL AND DATA
OUTLETS

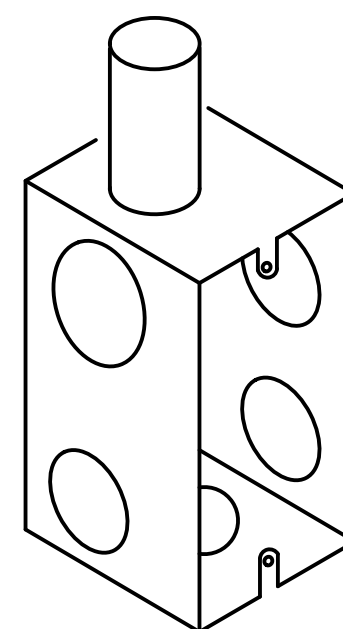


50mm X 100mm X 60mmD
SINGLE GANG BOX
20mm AND 25mm KNOCKOUTS

FOR SINGLE TELEPHONE,
ANALOG, AND TV OUTLETS

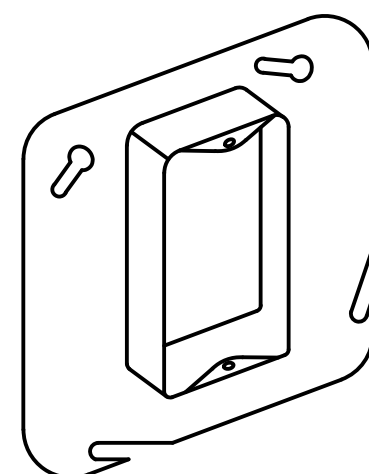

100mm SINGLE DEVICE MUD
RING VERTICAL FOR WALL
MOUNT PHONES AND
STANDARD OUTLETS

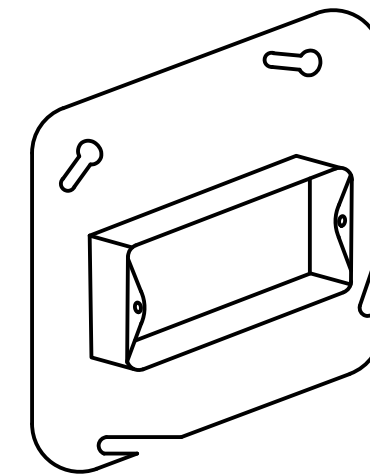

100mm SINGLE DEVICE MUD
RING HORIZONTAL FOR
COUNTERS

L1 **OUTLET BOX DETAILS**

STANDARD/FLOOR
DATA (2) PORTS

LABEL ALL PORTS,
SEE EXAMPLE,
THIS SHEET

The diagram shows a vertical rectangular patch panel with a double-line border. Inside, there are two RJ-45 ports, each represented by a square icon with internal wiring details. Above the top port and below the bottom port are empty rectangular boxes for labeling. An arrow points from the text 'THIS SHEET' to the left border of the panel.

(2) RJ-45 JACKS, CAT6 UTP
CABLE



DATA/TEL
(3) PORTS

VOICE

DATA

BLANK
COVER
PLATE

(3) RJ-45 JACKS, CAT6 UTP
CABLE



The diagram shows a rectangular unit with a double border. At the top, it is labeled "CATV (2) PORTS". Inside the unit, there are two ports: a "VIDEO" port represented by a circular symbol with concentric circles, and a "DATA" port represented by an RJ-45 jack symbol. There are also two horizontal rectangular slots, one above the VIDEO port and one below the DATA port.


(1) F-TYPE CONNECTOR, RG6
(1) RJ-45 JACK, CAT6 UTP CABLE




Diagram illustrating the wall mount telephone unit. The unit is shown with a rectangular frame. A label "WALL MOUNT TELEPHONE" is at the top. A label "MOUNTING LUGS" points to the top of the unit. A label "WALL PHONE MOUNTING LUGS (1) RJ-45, CAT5 UTP CABLE" points to the bottom of the unit.



INTERACTIVE WHITE
BOARD
(4) PORTS

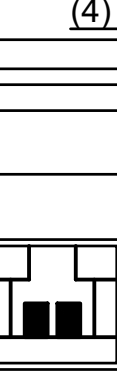

4) RJ-45 JACKS,
CAT5 UTP CABLE

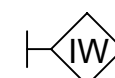


WIRELESS ACCESS
POINTS, INTERCOM, PA
DEVICES/CLOCKS, VTC
(1) PORT



The diagram shows a rectangular panel with a double border. In the center is a square RJ-45 jack port. The port has a central rectangular opening with two black vertical bars inside, representing the contacts. Above and below the port are horizontal rectangular slots, likely for screws or labels.

(1) RJ-45 JACK, CAT6 UTP CABLE

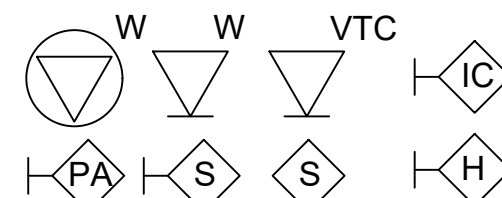


OUTLET LABELING

The diagram illustrates the structure of the label ***H103A-1A01-B-1**. The label is divided into segments by hyphens. Arrows point from each segment to its corresponding field name:

- *H103A** points to **ROOM NUMBER**
- 1** (after H103A) points to **FLOOR**
- A** points to ***TELECOM ROOM**
- 01** points to **SEQUENCE INDICATOR**
- B** points to **PORT NUMBER**
- 1** (after B) points to **PATCH PANEL**
- 1** (at the end) points to **RACK NUMBER**

Below the diagram, the full name for the first segment is provided:

*** ROOM H103A,
FIRST FLOOR,
TR1,
RACK 1,
PATCH PANEL B,
PORT 1**

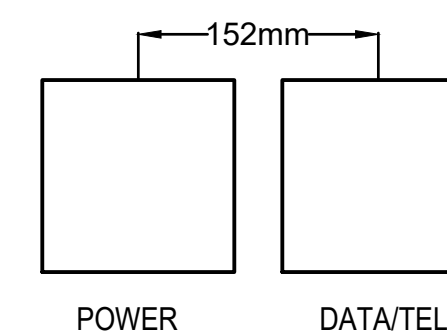

MOUNT COMMUNICATIONS OUTLETS (DATA, TV, VTC, ETC.) AND RELATED POWER OUTLET AS NOTED

A1 TELECOM OUTLET DETAILS

NONE

(A17) TYPICAL TLECOM/POWER OUTLET MOUNTING DETAIL

NC

US Army Corps
of Engineers®[illegible]

US ARMY CORPS OF ENGINEERS JAPAN DISTRICT, OKINAWA AREA OFFICE USAEJ-1, UNIT 35132 APO, AP 96374-5132	DESIGNED BY:	ISSUE DATE:
	DRAWN BY:	SOLICITATION NO.:
 SFSM INTERNATIONAL, INC. 501 SUMMER STREET, SUITE 620	CHECKED BY:	CONTRACT NO.:
	SUBMITTED BY:	SCALE: AS SHOWN
	SIZE:	FILE NAME:

KADENA AIR BASE, OKINAWA, JAPAN
VEHICLE MAINTENANCE SHOP
FY20 MCA PN77833


DETAILS

SHEET ID

T-501

INTERMEDIATE DESIGN

P
O
N
M
L
K
J
I
H
G
F
E
D
C
B
A

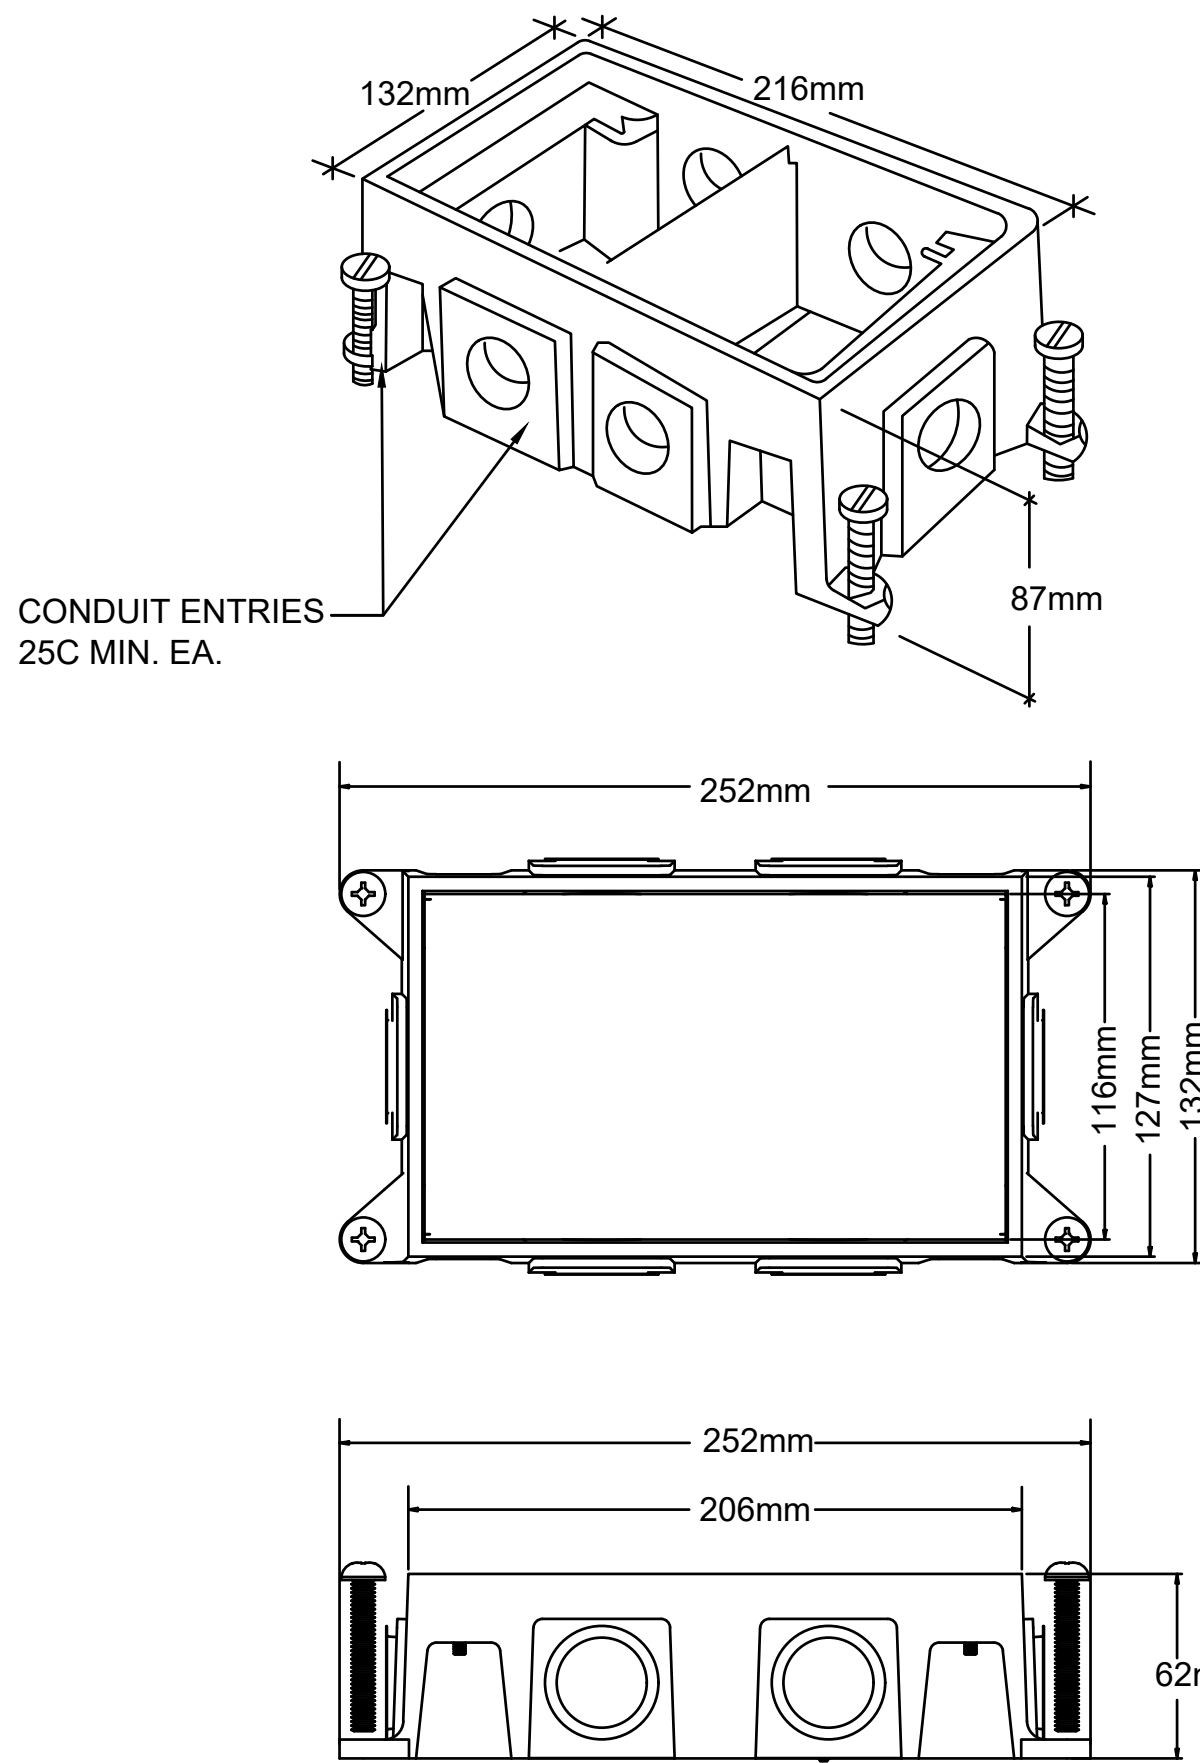


WATERTIGHT CONSTRUCTION FOR ON OR BELOW GRADE APPLICATION.


ACCEPTS INDUSTRY STANDARD AND PROPRIETARY DEVICES FROM A WIDE RANGE OF MANUFACTURERS TO PROVIDE A SEAMLESS AND AESTHETICALLY PLEASING INTERFACES FOR VOICE, DATA, AUDIO, AND VIDEO APPLICATIONS AT THE POINT-OF-USE.

TWO GANG CAST IRON FLOOR BOX - FULLY ADJUSTABLE

TECHINCAL SPECIFICATIONS			
CONDUIT OPENINGS	CUBIC INCH CAPACITY	ADJUSTMENT BEFORE POUR	ADJUSTMENT AFTER POUR
(6) (25mm)	CUBIC INCH CAPACITY	ADJUSTMENT BEFORE POUR	ADJUSTMENT AFTER POUR

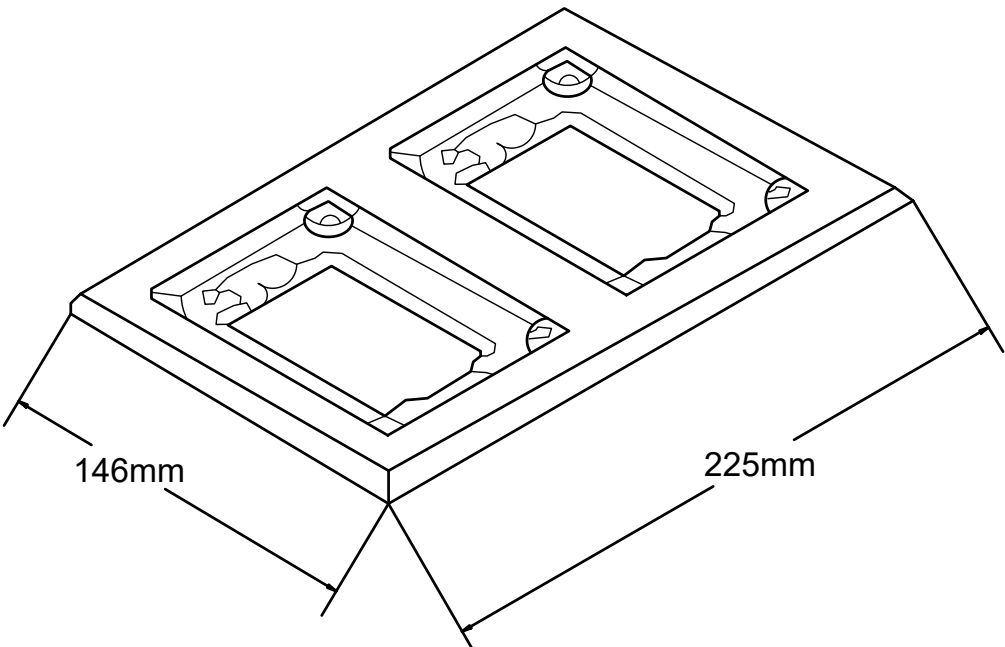

TWO GANG BRASS CARPET FLANGE

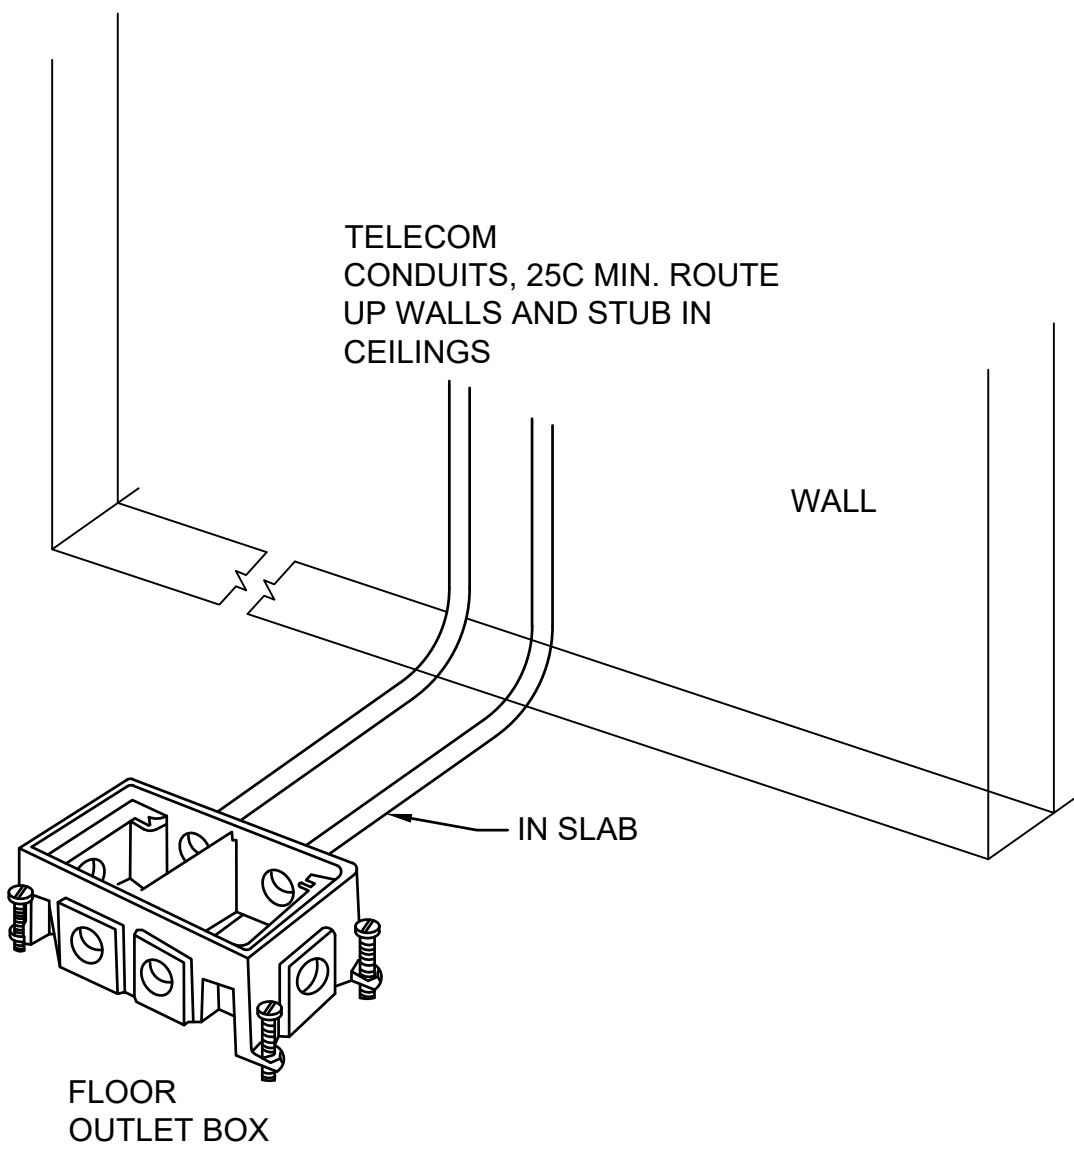

B5 FLOOR DATA OUTLET DETAIL

H3 FLOOR DATA OUTLET BOX DETAIL

US Army Corps of Engineers®

DESIGNED BY:		ISSUE DATE:	
DRAWN BY:		SOLICITATION NO.:	
CHECKED BY:		CONTRACT NO.:	
SUBMITTED BY:		SCALE:	
SIZE:		FILE NAME:	
ISO A1		AS SHOWN	

US ARMY CORPS OF ENGINEERS
JAPAN DISTRICT, OKINAWA AREA OFFICE
USAED-J UNIT 35132
APO, AP 96374-5132

SSEFM
SSEFM INTERNATIONAL, INC.
501 SUMNER STREET, SUITE 620
HONOLULU, HAWAII 96817

KADENA AIR BASE, OKINAWA, JAPAN
VEHICLE MAINTENANCE SHOP
FY20 MCA PN77833


DETAILS

SHEET ID


T-502

INTERMEDIATE DESIGN


—
O —
N —
M —
L —
K —
J —
I —
H —
G —
F —
E —
D —
C —
B —
A

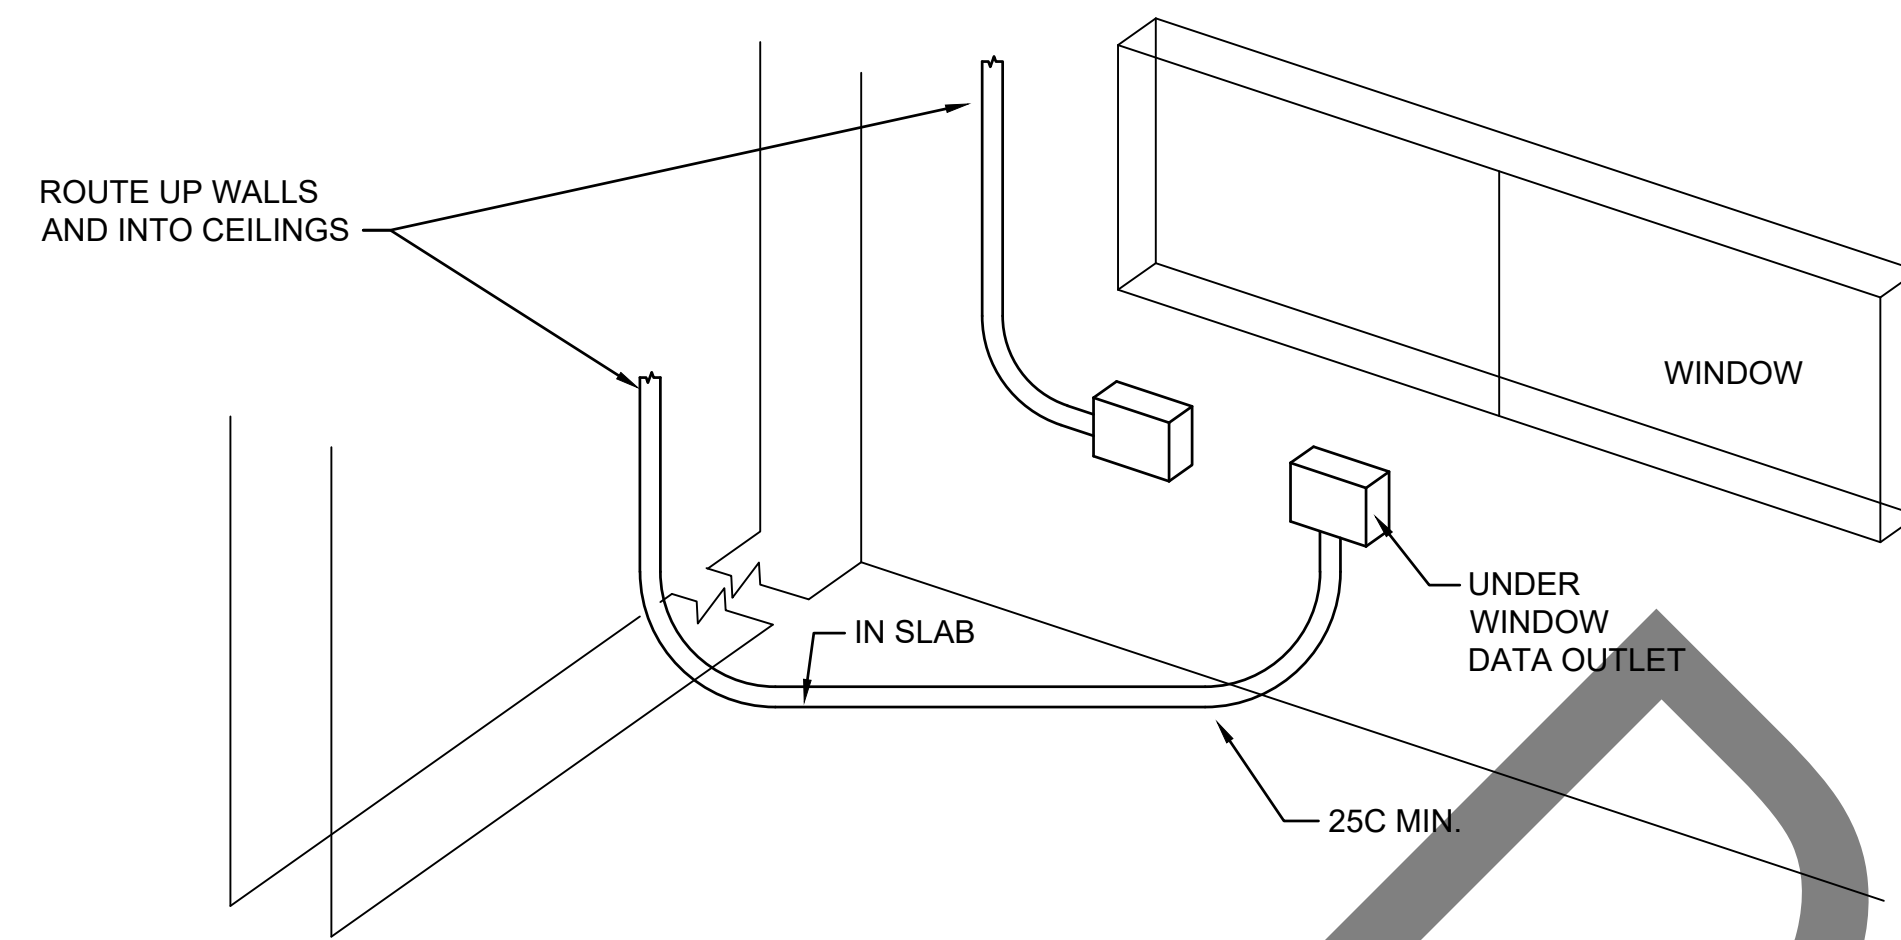


K4 FLOOR BOX TO DATA OUTLET DETAIL

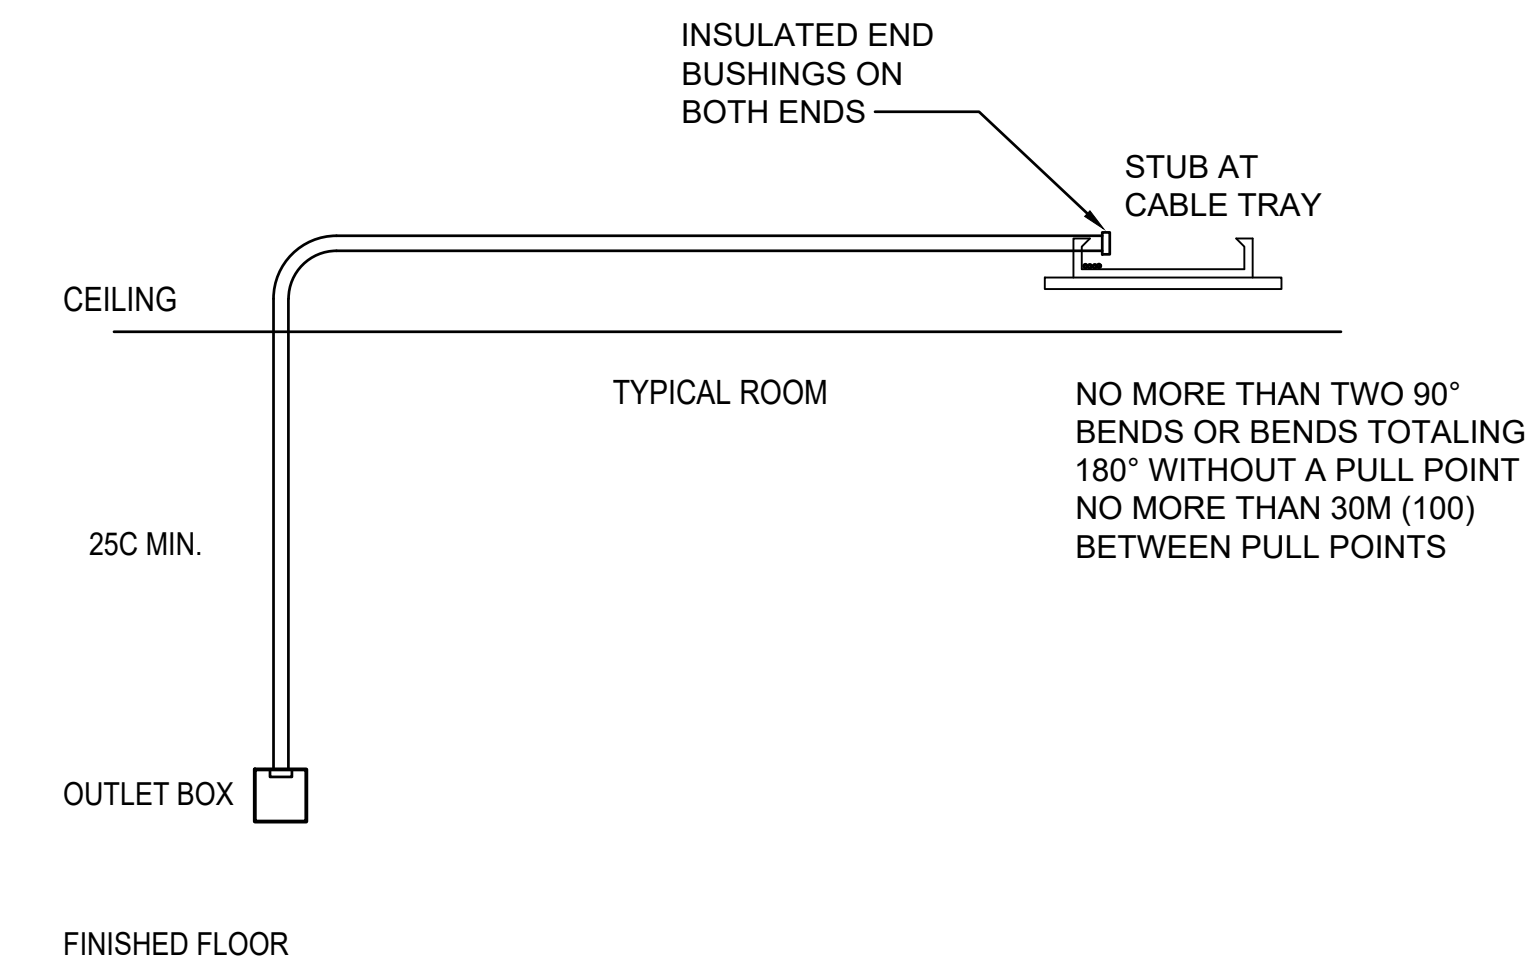

K13 CABLE SUPPORT DETAIL

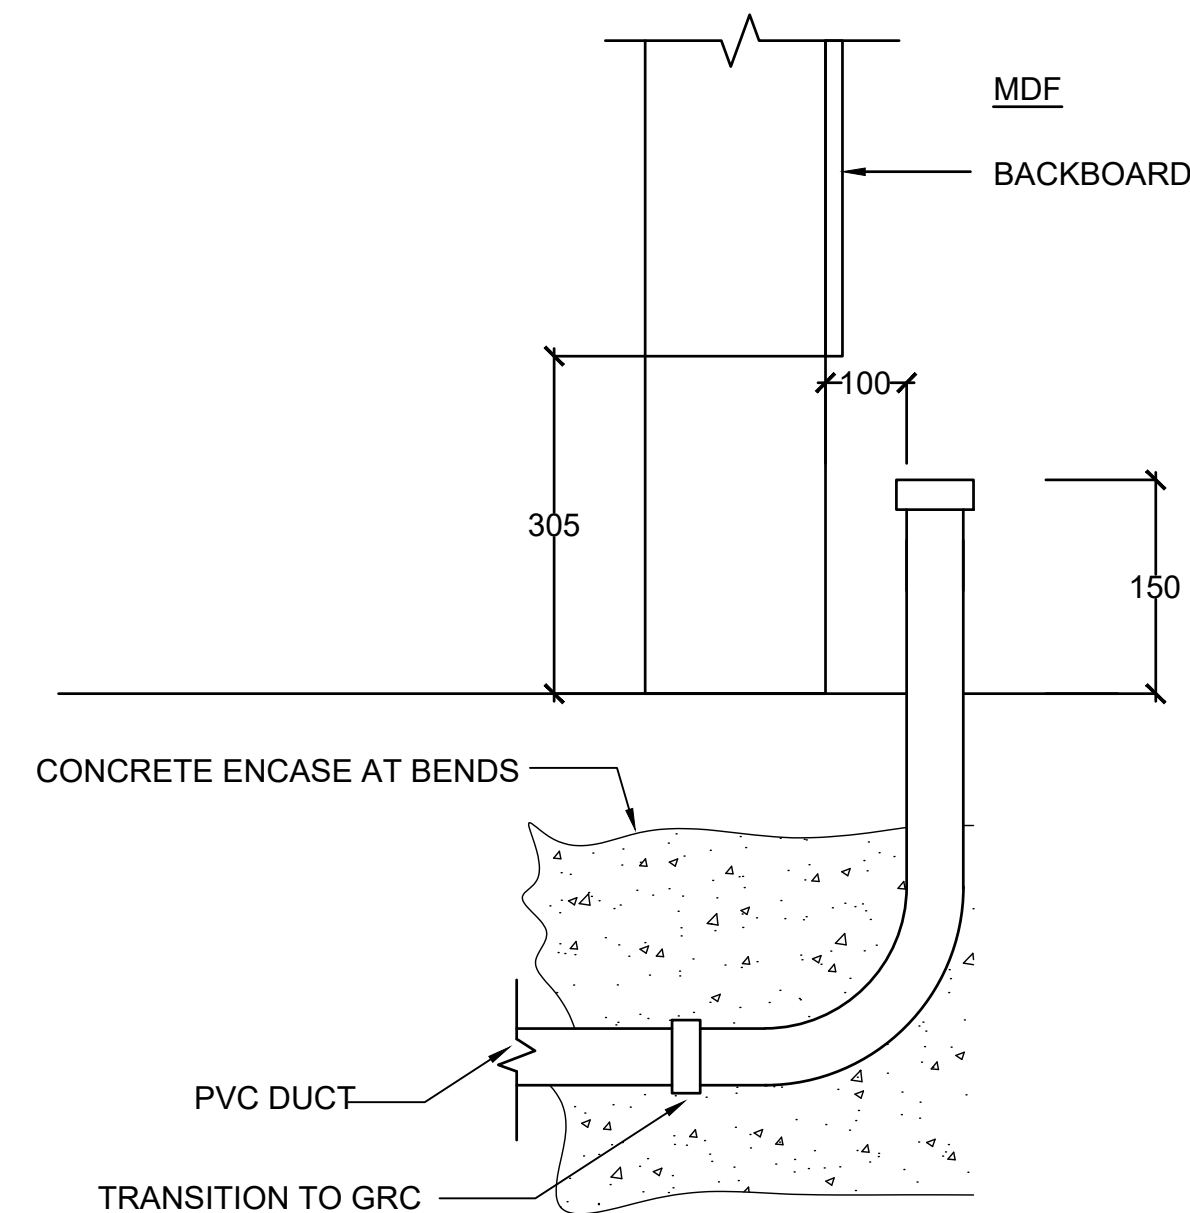

C5 DUCT RISER DETAIL

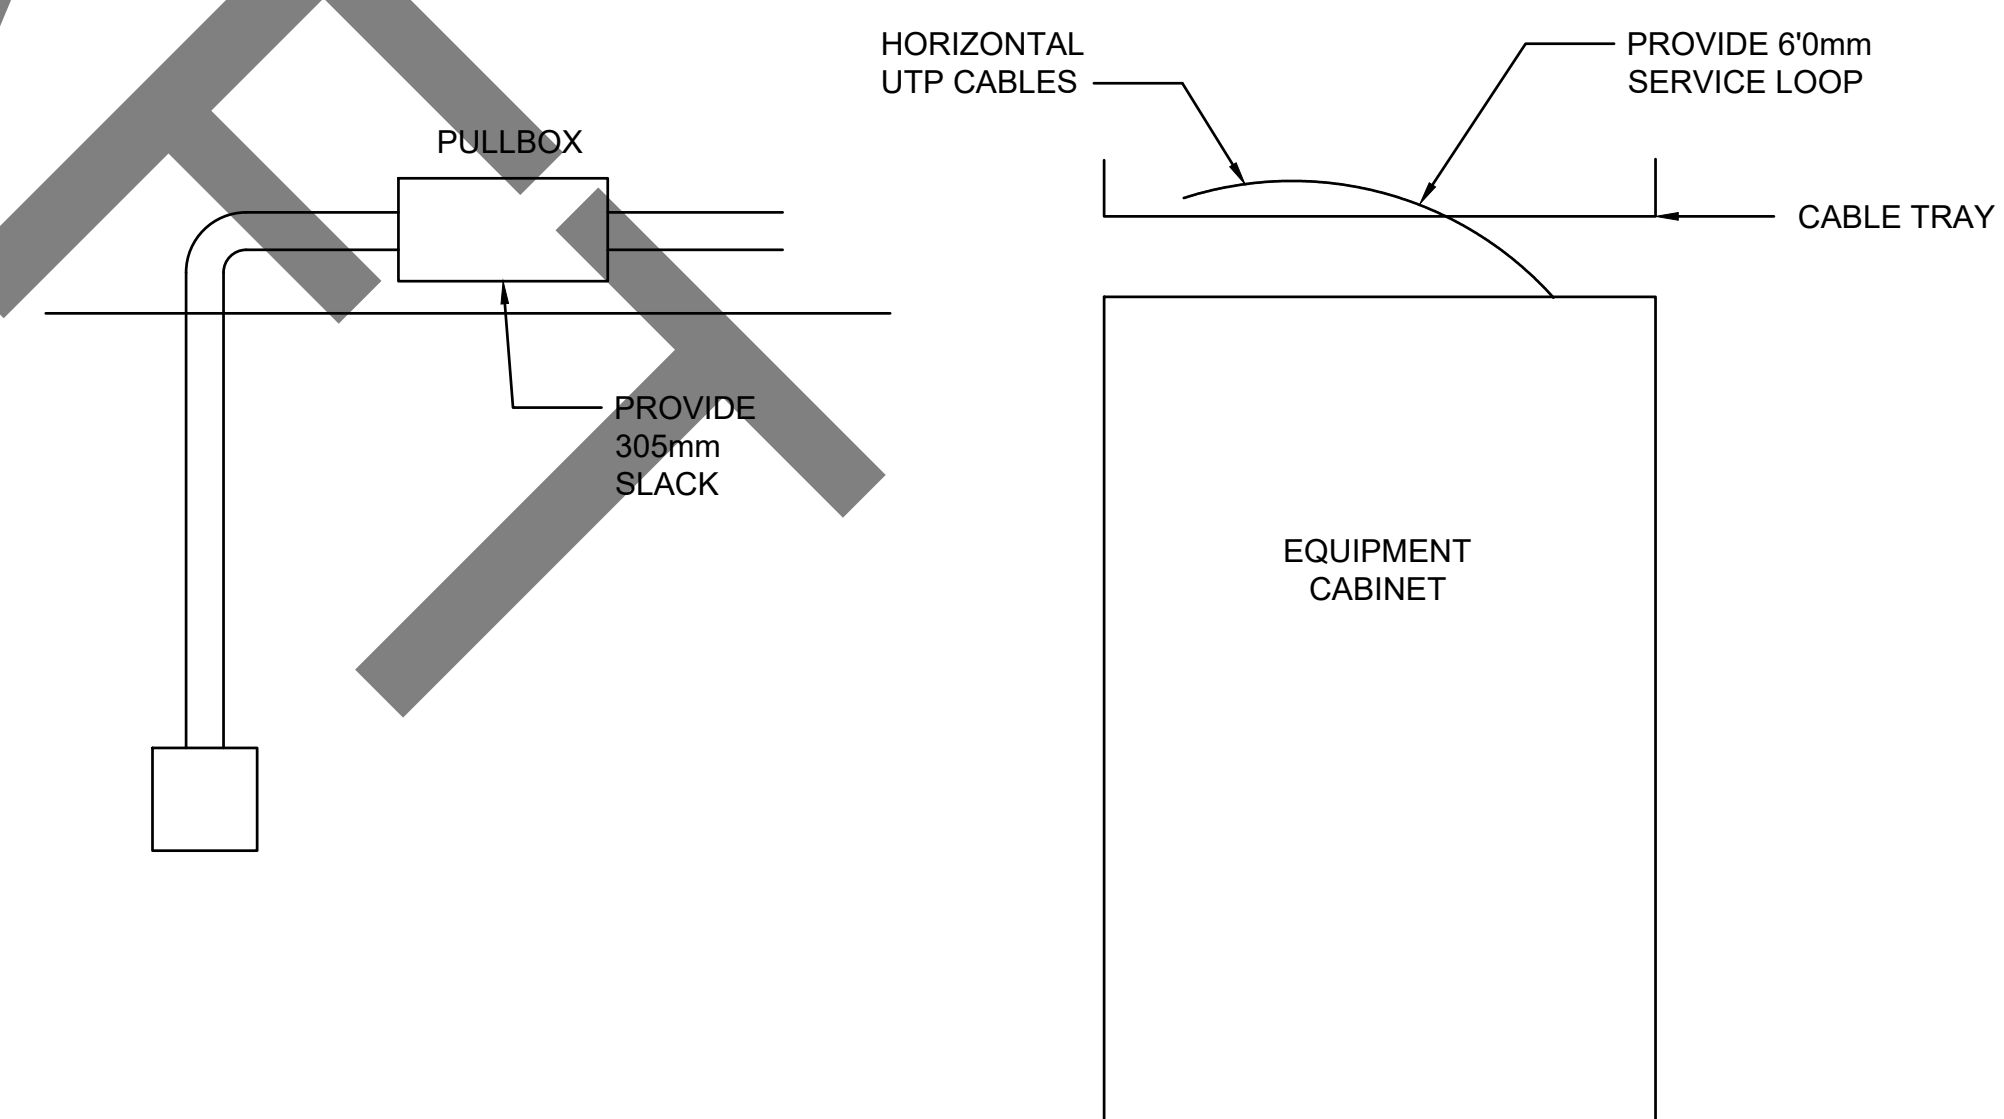

C14 FO SERVICE LOOP DETAIL



**U.S. Army Corps
of Engineers®**

[illegible]

JAPAN DISTRICT, OKINAWA AREA OFFICE		SOLICITATION NO.:	
USAD-J UNIT 35132		DRAWN BY:	
APO, AP 96374-15132		CHECKED BY:	
		SUBMITTED BY:	
SSPM INTERNATIONAL, INC.		AS: SHOWN	
500 KALANANU'U DRIVE, #20		FILE NAME:	
HONOLULU, HAWAII 96817		SIZE: ISO A1	

MADEIRA AIR BASE, OKINAWA, JAPAN
VEHICLE MAINTENANCE SHOP
FY20 MCA PN77833

SHEET ID

T-503

INTERMEDIATE DESIGN

[illegible]

JAPAN DISTRICT, OKINAWA AREA OFFICE USAED-J UNIT 35132 APO, AP 96374-5132		 SSFM INTERNATIONAL, INC 501 SUMMER STREET, SUITE 620
DRAWN BY:	SOLICITATION NO.:	
CHECKED BY:	CONTRACT NO.:	
SUBMITTED BY:	SCALE: AS SHOWN	
SIZE:	FILE NAME:	

MAJENKAR BASEL CHINA JAPAN
VEHICLE MAINTENANCE SHOP
FYZO MCA PNT7833

SHEET ID

T-504



NONE

GROUNDING AND BONDING CONDUCTOR LABEL




CABLE TRAY SYSTEM SHALL BE
INSTALLED IAW WITH THE
FOLLOWING STANDARDS:



- ## 1. NEMA VE1 METAL CABLE TRAY SYSTEMS

CABLE TRAY SHOULD NOT BE INSTALLED DIRECTLY ON TOP OF THE EQUIPMENT CABINET. CABLE TRAY SHOULD NOT BE INSTALLED WITHIN 12" OF THE CEILING OR ANY OTHER OBSTACLES. HORIZONTAL TEE SUPPORT SHOULD BE USED FOR ALL JUNCTIONS. CABLE TRAY SHOULD NOT OVERLAP EACH OTHER.


A — B — C — D — E — F — G — H — I — J — K — L — M — N — O — P

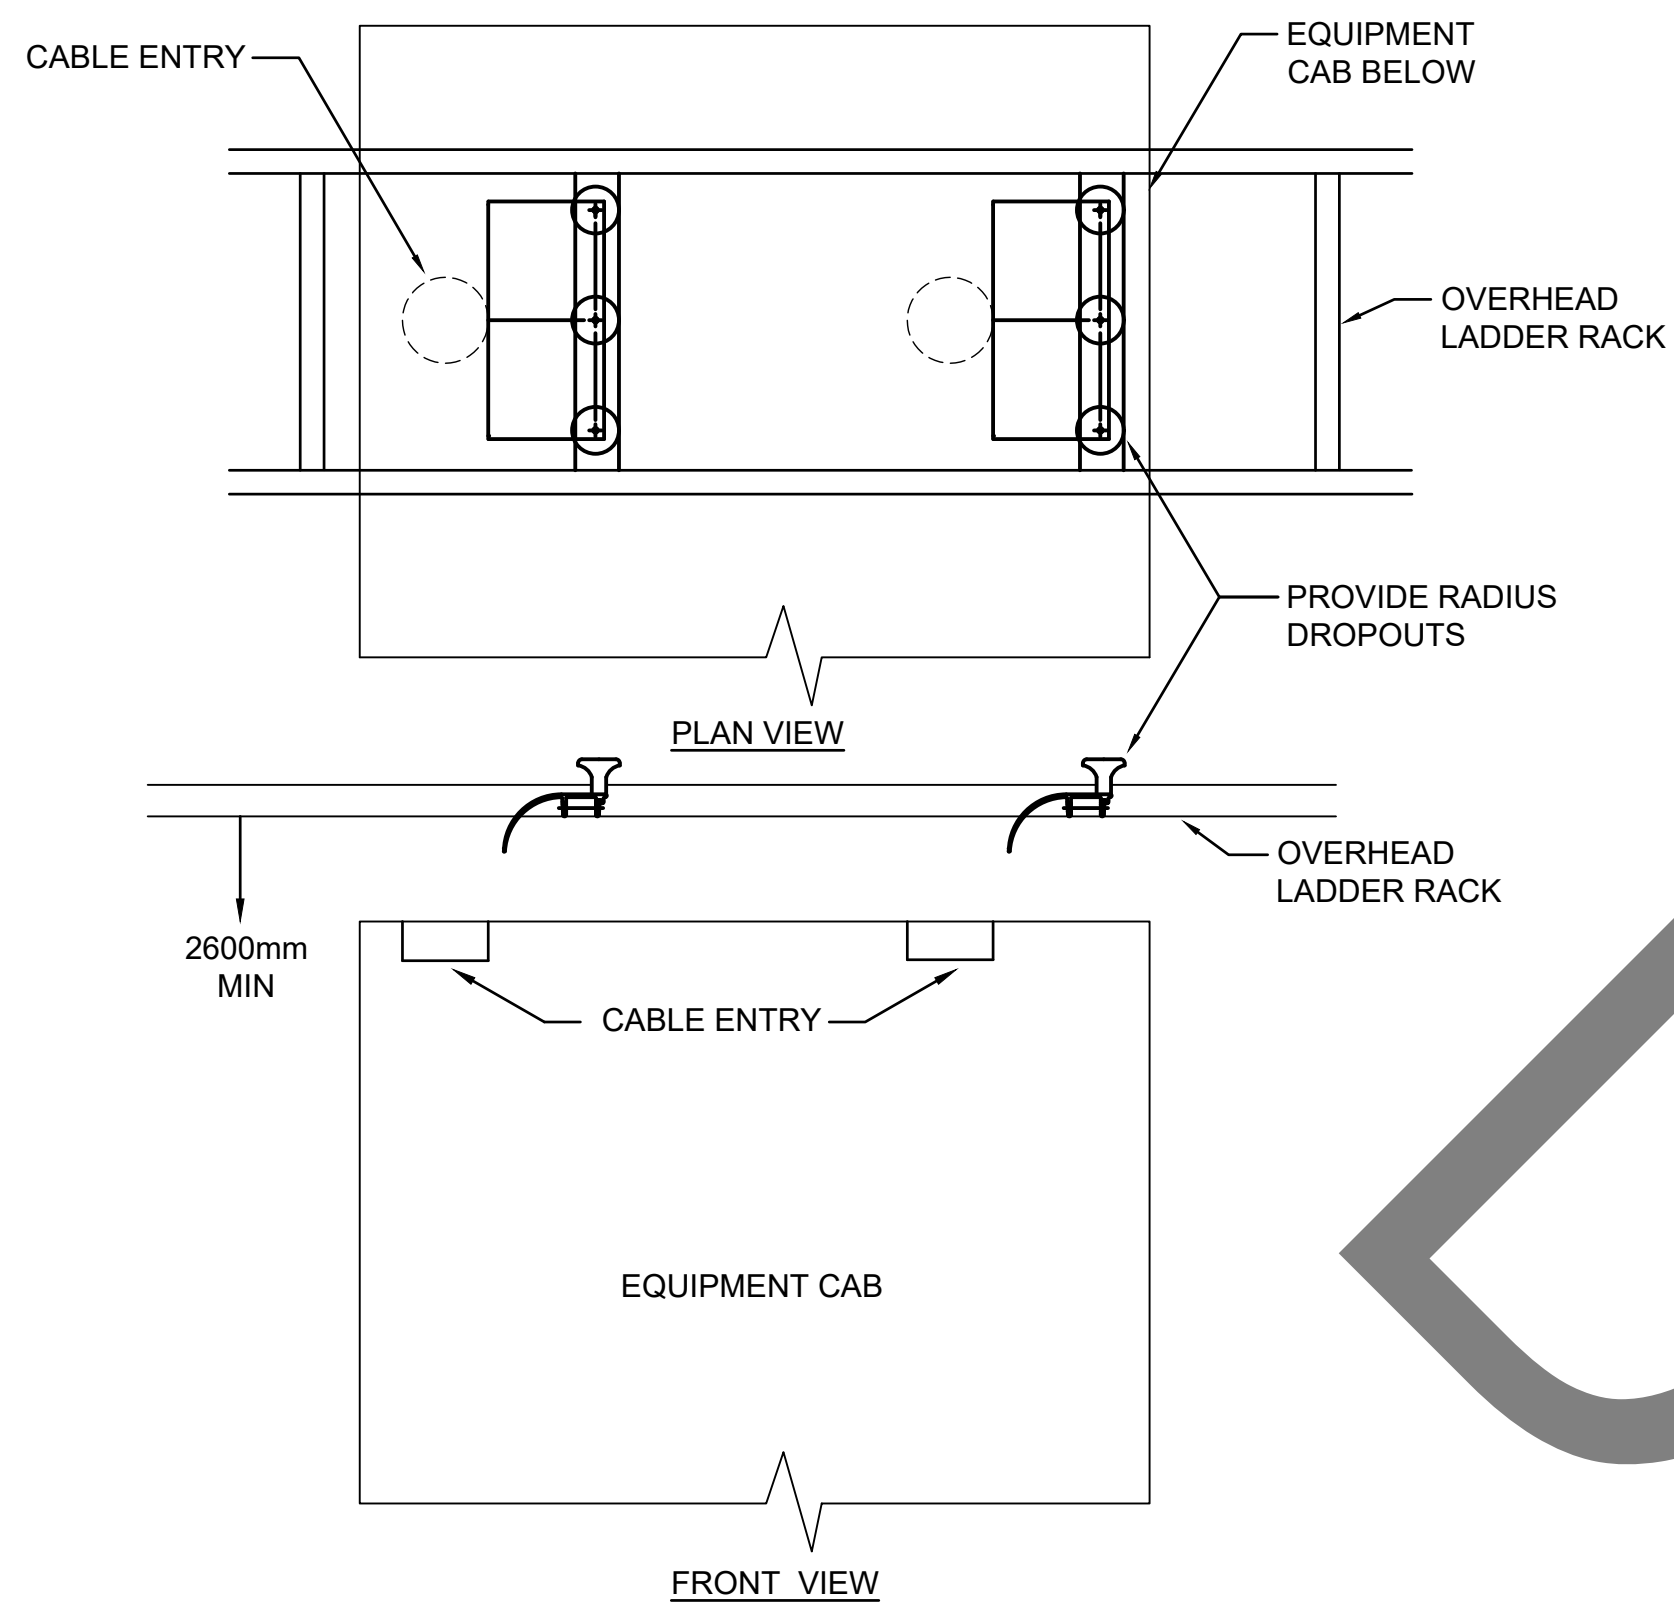


13 CABLE TRAY TO EQUIPMENT CABINET TRANSITIONS

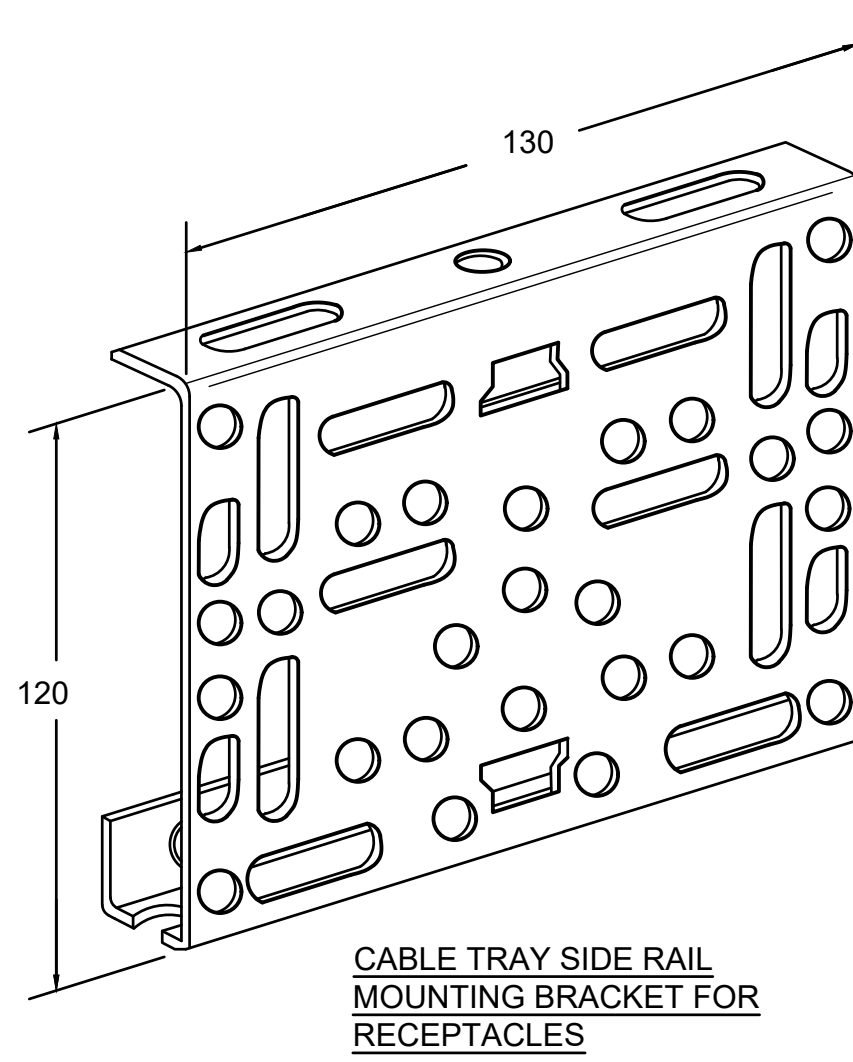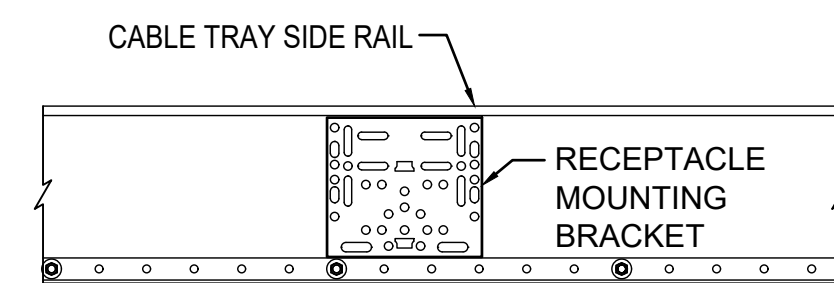

C3 LADDER RACK POWER OUTLET MOUNTING DETAIL

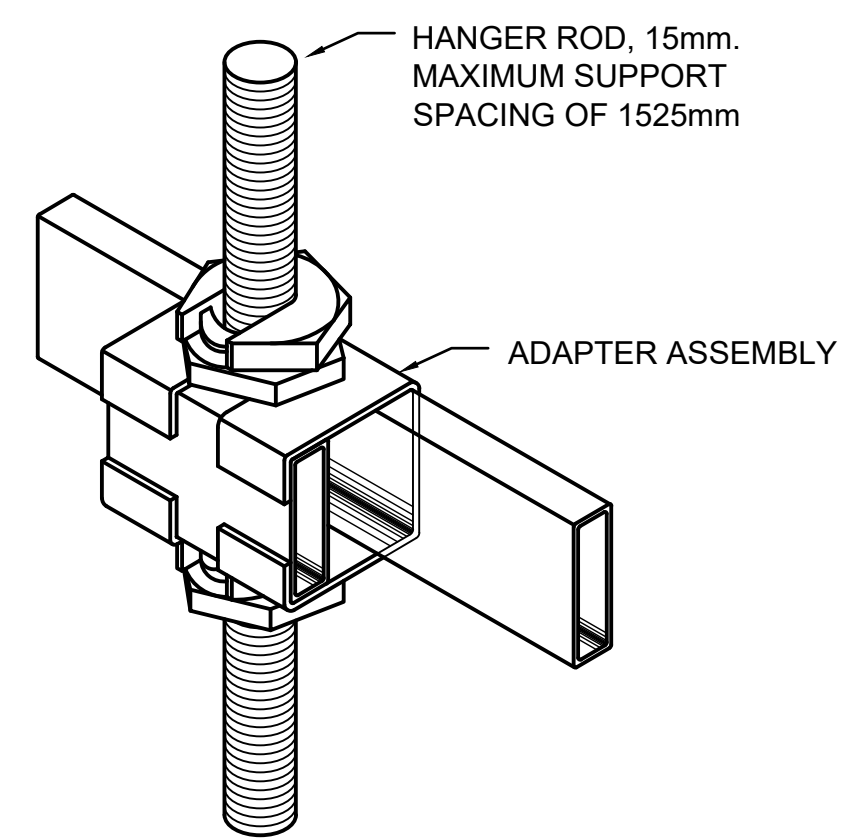


OPEN AREA MOUNTING

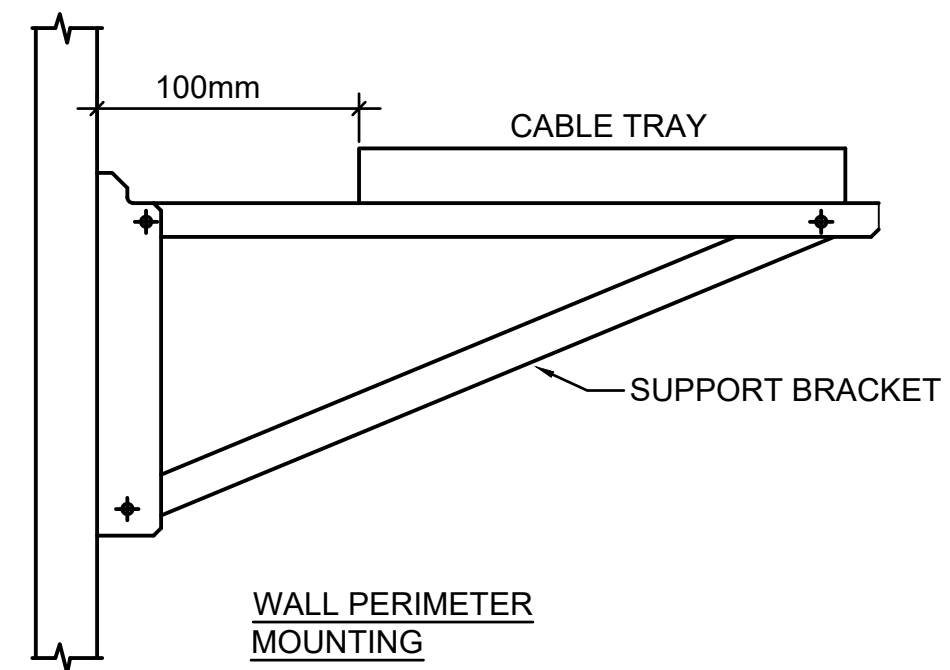


WALL PERIMETER MOUNTING


114	SUPPORT BRACKET AND OVERHEAD CABLE TRAY SUPPORT	NONE
-----	---	------

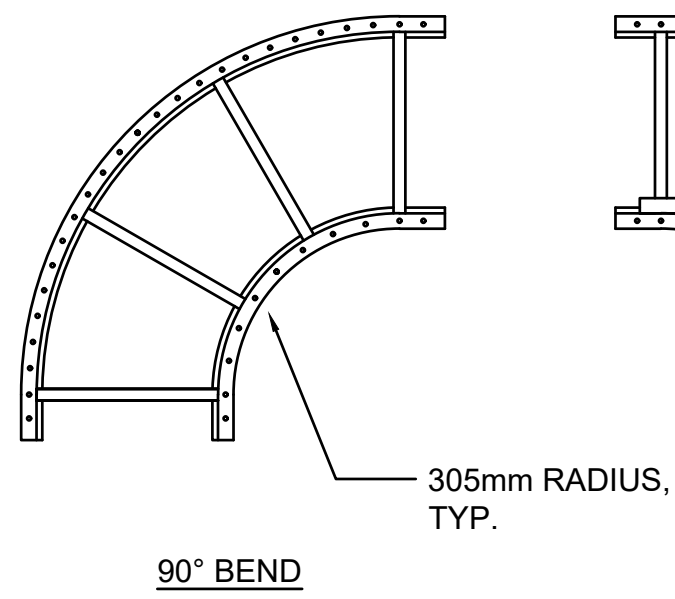

90° BEND

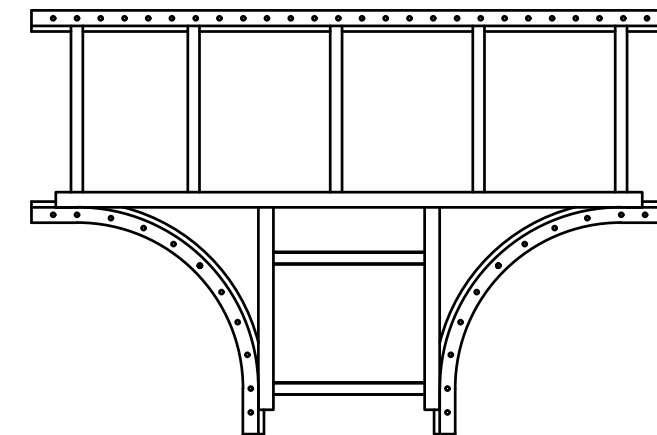

"TEE"

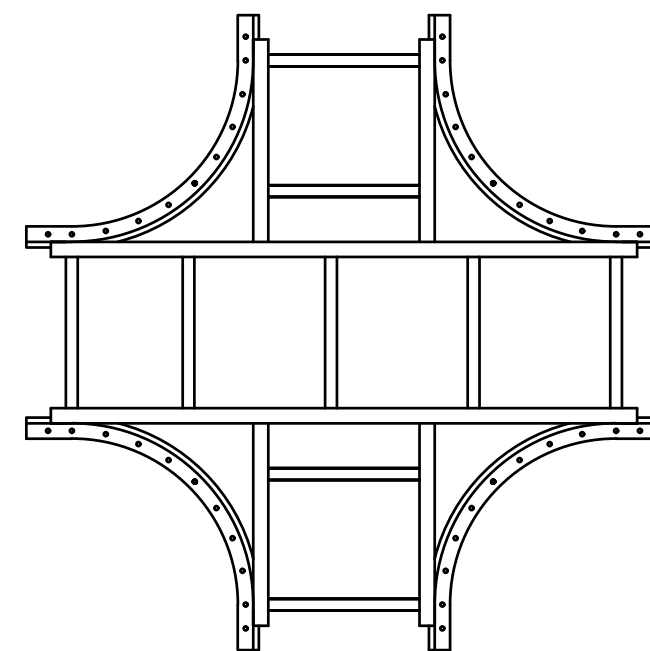

"CROSS"

C11 HORIZONTAL TURN DETAILS



U.S. Army Corps
Engineers®


[illegible][illegible]

FY20 MCA PN77833

SHEET ID

T-505

INTERMEDIATE DESIGN

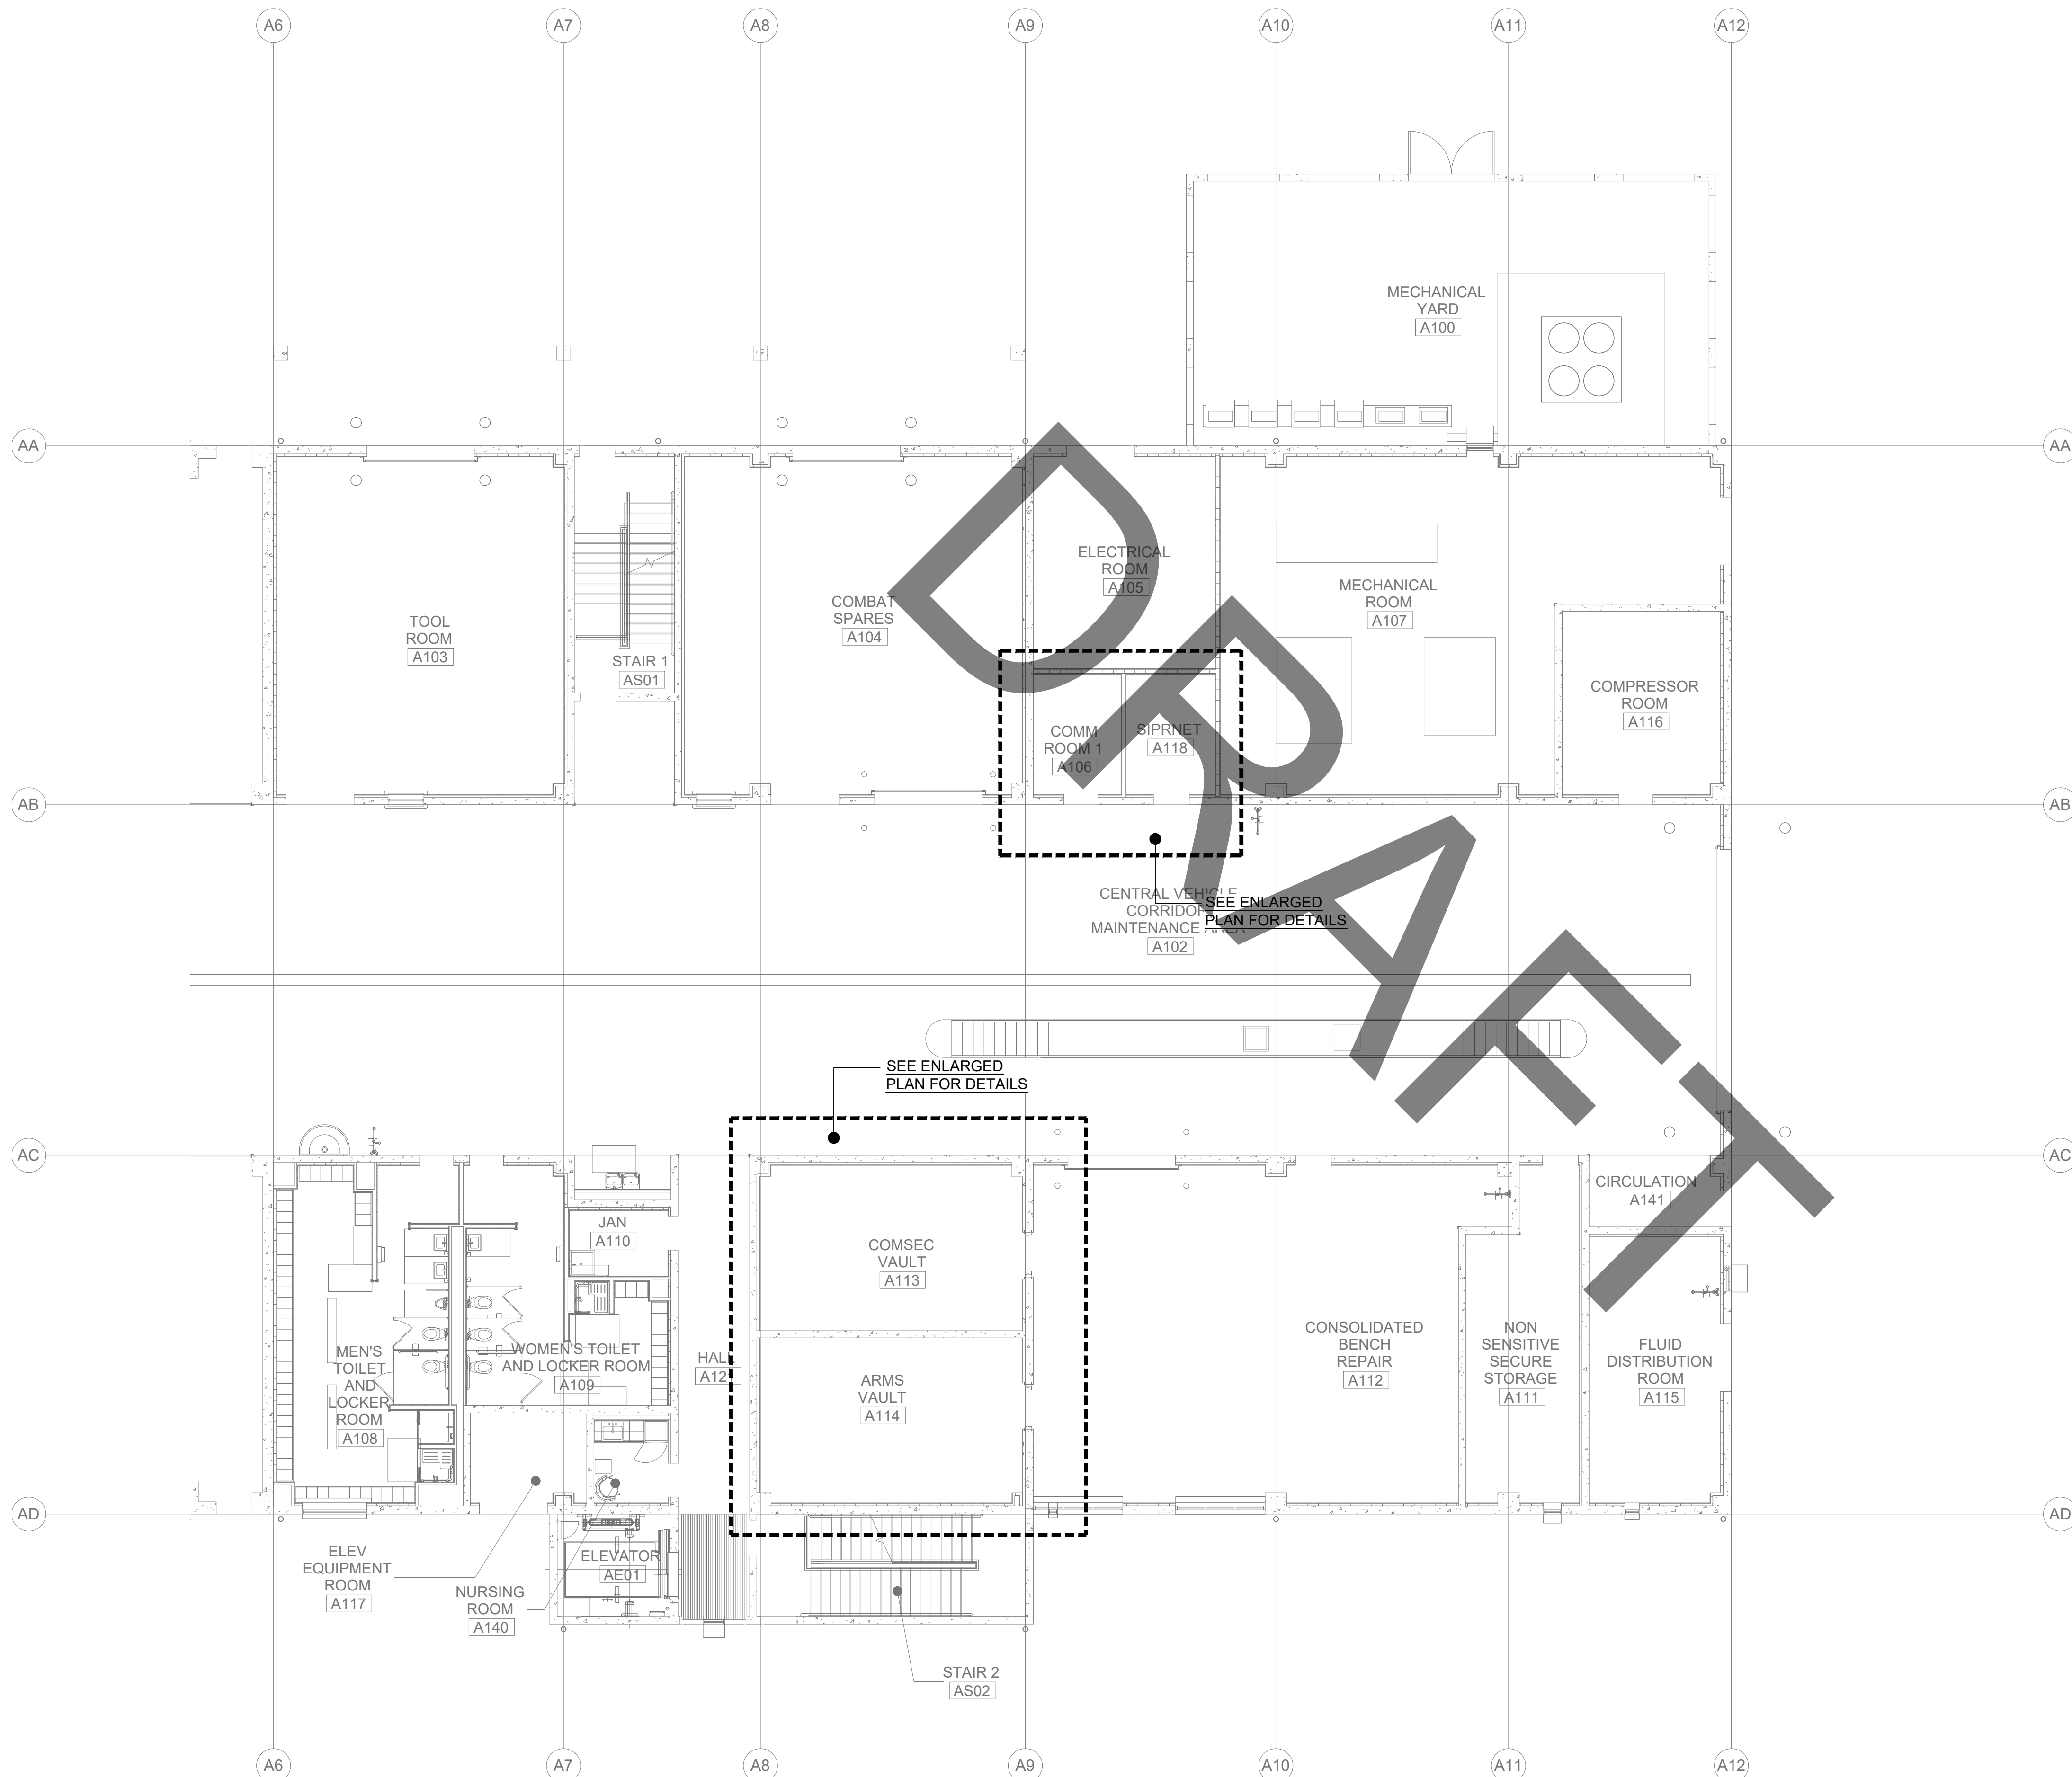

A1 VMS - PARTIAL FIRST FLOOR SECURITY PLAN - ZONE B (CLIN 0001)
1:100

GENERAL NOTES

US Army Corps
of Engineers®[illegible]


LEGEND

US ARMY CORPS OF ENGINEERS JAPAN DISTRICT, OKINAWA AREA OFFICE USAEJ-1, UNIT 35132 APO, AP 96374-4132		DESIGNED BY: DRAWN BY: CHECKED BY: SUBMITTED BY:	ISSUE DATE: SOLICITATION NO.: CONTRACT NO.: SCALE: AS SHOWN
		SPM INTERNATIONAL, INC. 551 SUMNER STREET, SUITE 620	FILE NAME: SIZE:



CLIN 0001

KEY PLAN

VMS - LEVEL 1
N.T.S.

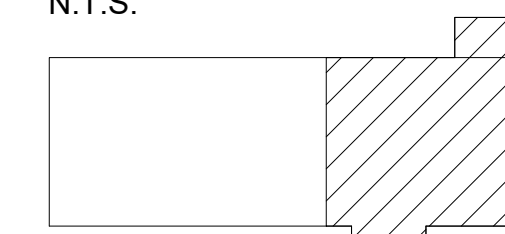

GRAPHIC SCALE

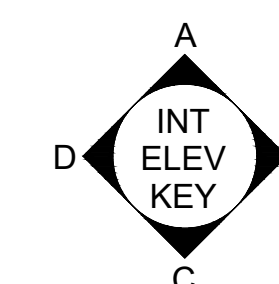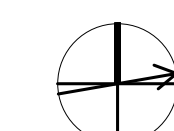PLAN
NORTH

SCALE: 1 : 100

ALL DIMENSIONS AND/OR DIMENSIONS SHOWN IN
CALLOUT/ NOTES ARE IN MILLIMETERS UNLESS
OTHERWISE NOTED.

KADENA AIR BASE, OKINAWA, JAPAN
VEHICLE MAINTENANCE SHOP
FY20 MCA PN77833


SHEET ID

TYA112



(A1) VMS - PARTIAL SECOND FLOOR SECURITY PLAN - ZONE B (CLIN 0001)
1:100

GENERAL NOTES

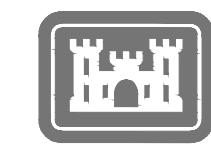

US Army Corps
of Engineers®

Item	Value	Unit
1. 1000	1000	1000
2. 1000	1000	1000
LEGEND

US ARMY CORPS OF ENGINEERS JAPAN DISTRICT, OKINAWA AREA OFFICE USAED-J, UNIT 35132 APO, AP 96374-5132	ISSUE DATE:	
	DESIGNED BY:	
	DRAWN BY:	
	SOLICITATION NO.:	
	CHECKED BY:	CONTRACT NO.:
	SUBMITTED BY:	SCALE: AS SHOWN
	SIZE: 1/8" = 1'-0"	FILE NAME:

KADENA AIR BASE, OKINAWA, JAPAN
VEHICLE MAINTENANCE SHOP
FY20 MCA PN77833

SHEET ID


TYA114

INTERMEDIATE DESIGN

CLIN 0001

KEY PLAN

VMS - LEVEL 2
N.T.S.

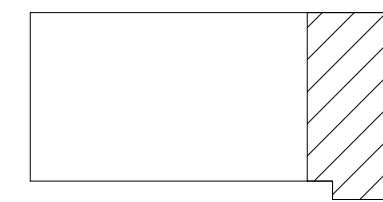


GRAPHIC SCALE



SCALE: 1 : 100



ALL DIMENSIONS AND/OR DIMENSIONS SHOWN IN
CALLOUT/ NOTES ARE IN MILLIMETERS UNLESS
OTHERWISE NOTED.

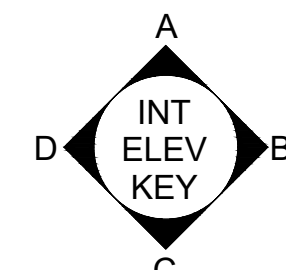

GENERAL NOTES



U.S. Army Corps
Engineers®


[illegible]

JAPAN DISTRICT, OKINAWA AREA OFFICE		SOLICITATION NO.:	
USED-J-1 UNIT 35132		DRAWN BY:	
APO, AP 96374-5132		CHECKED BY:	
		CONTRACT NO.:	
SSFM INTERNATIONAL, INC.		SUBMITTED BY:	
501 KALANANUE AVE #20		AS SHOWN	
HONOLULU, HAWAII 96817		SIZE:	FILE NAME:
		ISO A1	


SHEET ID

TYA401


INTERMEDIATE DESIGN

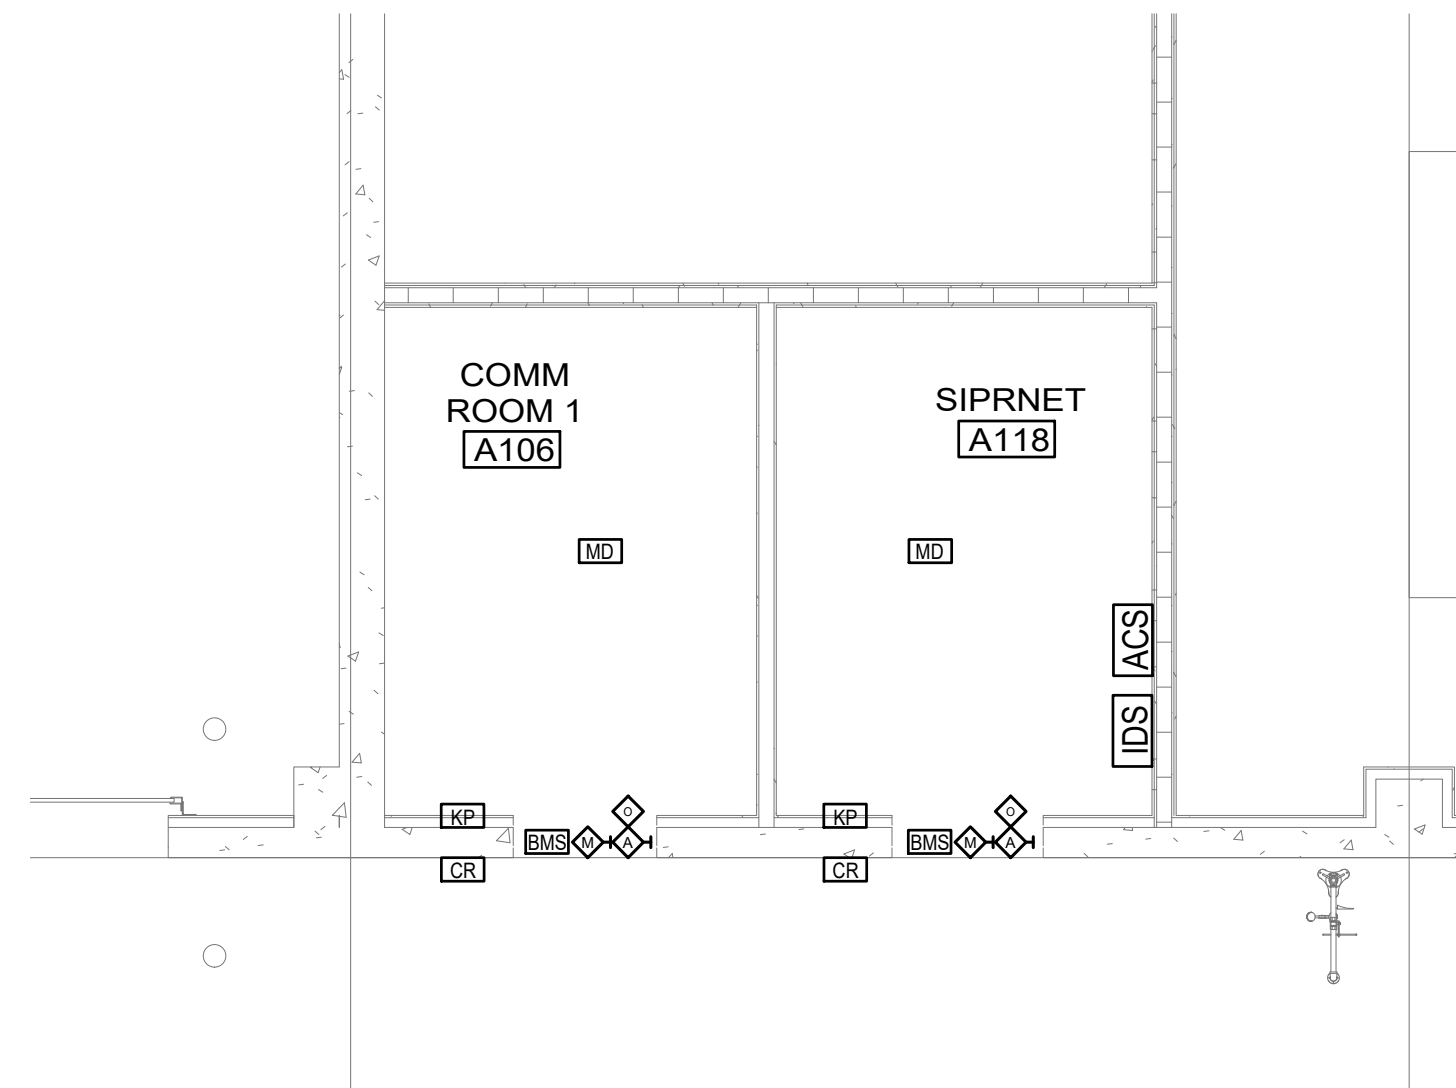

K4 VMS - ENLARGED SECURITY PLAN (1ST FLOOR)
1:50

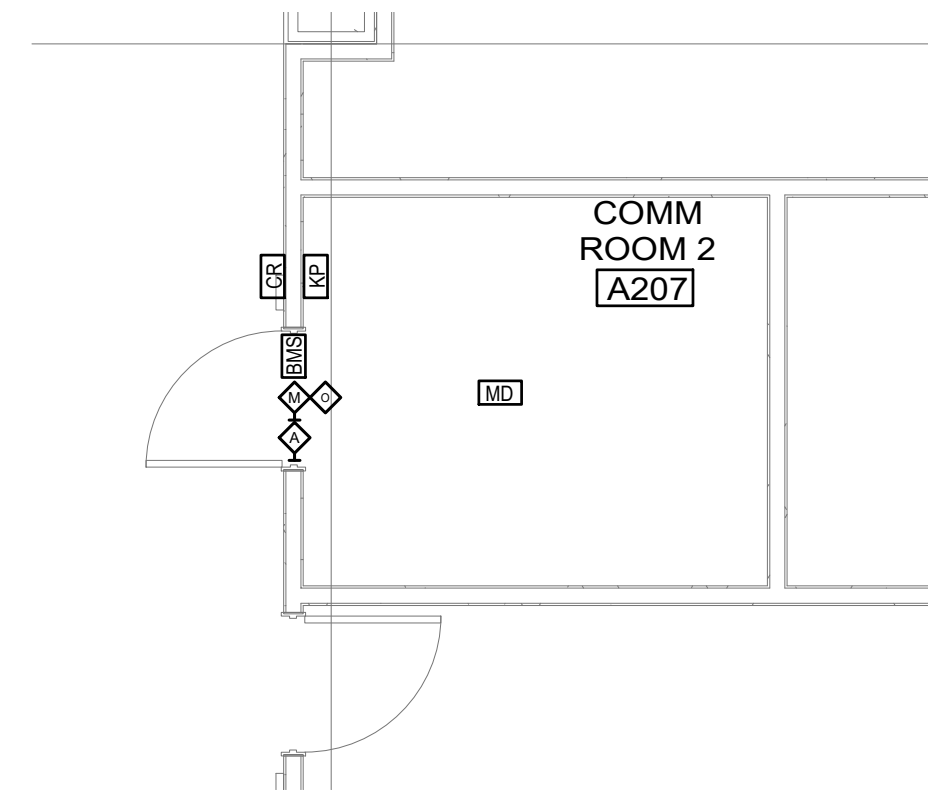

K4 VMS - ENLARGED SECURITY PLAN (2ND FLOOR)

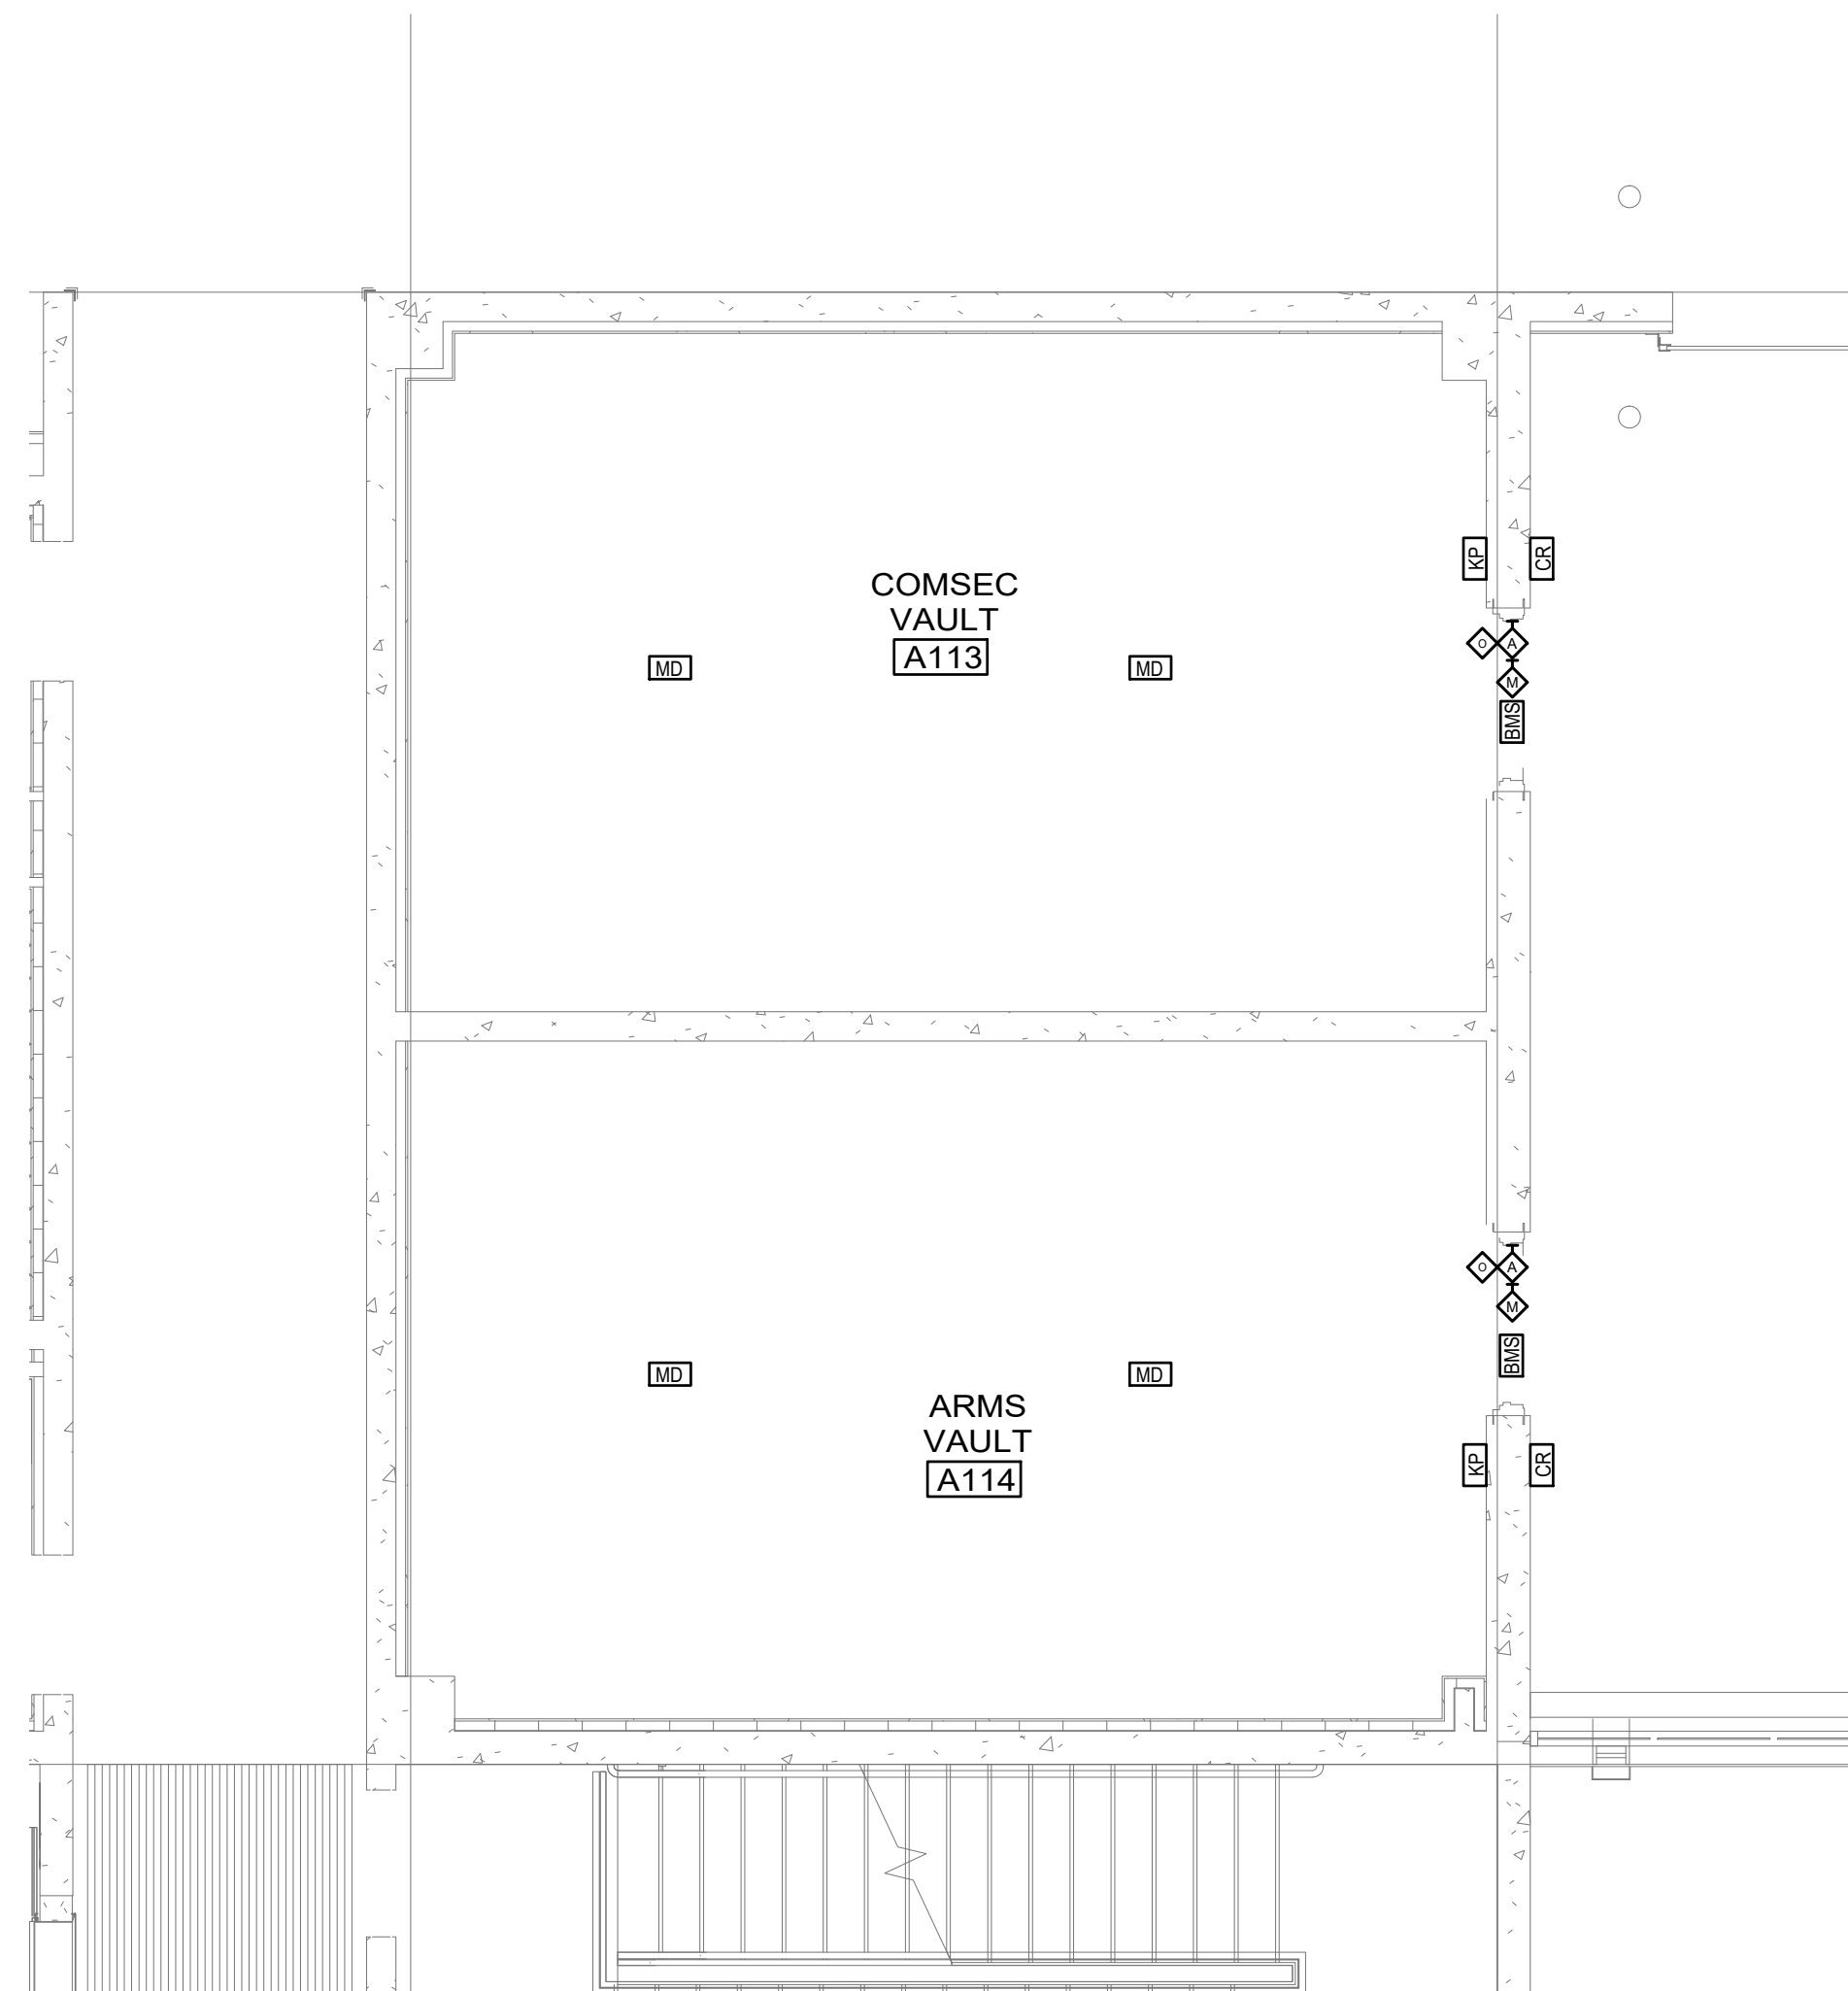

K4 VMS - ENLARGED SECURITY PLAN (1ST FLOOR)
1:50

ACCESS CONTROL SYSTEM (ACS)

ACP	ACCESS CONTROL PANEL
A	ELECTRIFIED DOOR LOCK
M	MAGNETIC DOOR POSITION SWITCH
CR	CARD READER
O	MOTION SENSOR DOOR RELEASE

INTRUSION DETECTION SYSTEM (IDS)

IDS	INTRUSION DETECTION SYSTEM (IDS) PANEL
BMS	IDS BALANCED MAGNETIC DOOR SWITCH
KP	IDS KEY PAD
MD	IDS PASSIVE INFRARED MOTION SENSOR, DOWN VIEW
	IDS PASSIVE INFRARED MOTION SENSOR, 360 VIEW

CLIN 0001

GRAPHIC SCALE



SCALE: 1 : 50


ALL DIMENSIONS AND/OR DIMENSIONS SHOWN IN
CALLOUT/ NOTES ARE IN MILLIMETERS UNLESS
OTHERWISE NOTED.

11

1. IDS SYSTEM SHALL BE INSTALLED IN ACCORDANCE WITH ICD 705 AND BE ABLE TO COMMUNICATE WITH BLDG 705 / 18 SECURITY OFFICE. TYPES OF SENSORS AND MOTION DETECTORS ARE LISTED IN THE ICD-705.
2. THE CONTRACTOR SHALL BE RESPONSIBLE TO VERIFY THE PROPER DEVICE COVERAGE FOR THE PROTECTED SPACES.
3. ALL IDS SYSTEMS SHALL BE THE SAME MANUFACTURE AND SHOULD BE A COMPLETE FUNCTIONAL SYSTEM, INCLUDE DEVICES, CONTROL PANELS AND WIRING PROVIDED BY THE CONTRACTOR.
4. IDS INSTALLER SHOULD BE UL2050 CERTIFIED AND THEY SHALL FOLLOW ICD 705 AND UL 634.



CLIN 0001

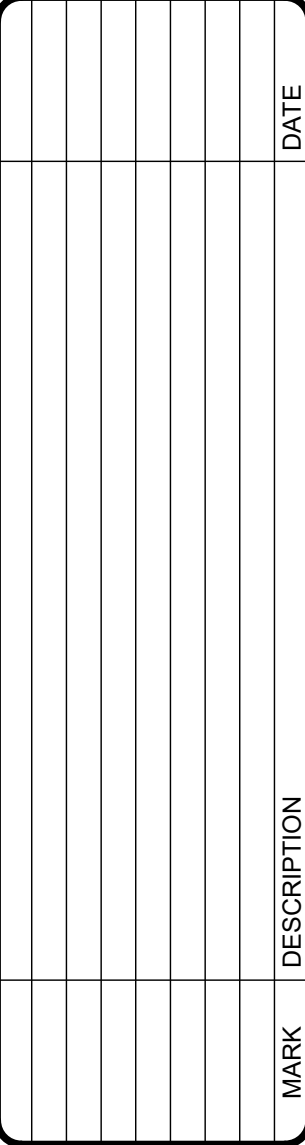

DESIGNED BY: US ARMY CORPS OF ENGINEERS JAPAN DISTRICT, OKINAWA AREA OFFICE USAED-J, UNIT 35132 APO, AF 96374-5132		ISSUE DATE: SOLICITATION NO.: CONTRACT NO.:	
DRAWN BY: CHECKED BY:		SCALE: AS SHOWN	
SUBMITTED BY:		FILE NAME: ISO A1	


KADENA AIR BASE, OKINAWA, JAPAN
VEHICLE MAINTENANCE SHOP
FY20 MCA PN77833

TYA601

INTERMEDIATE DESIGN

1.101

— P
— O
— N
— M
— L
— K
— J
— I
— H
— G
— F
— E
— D
— C
— B
— A

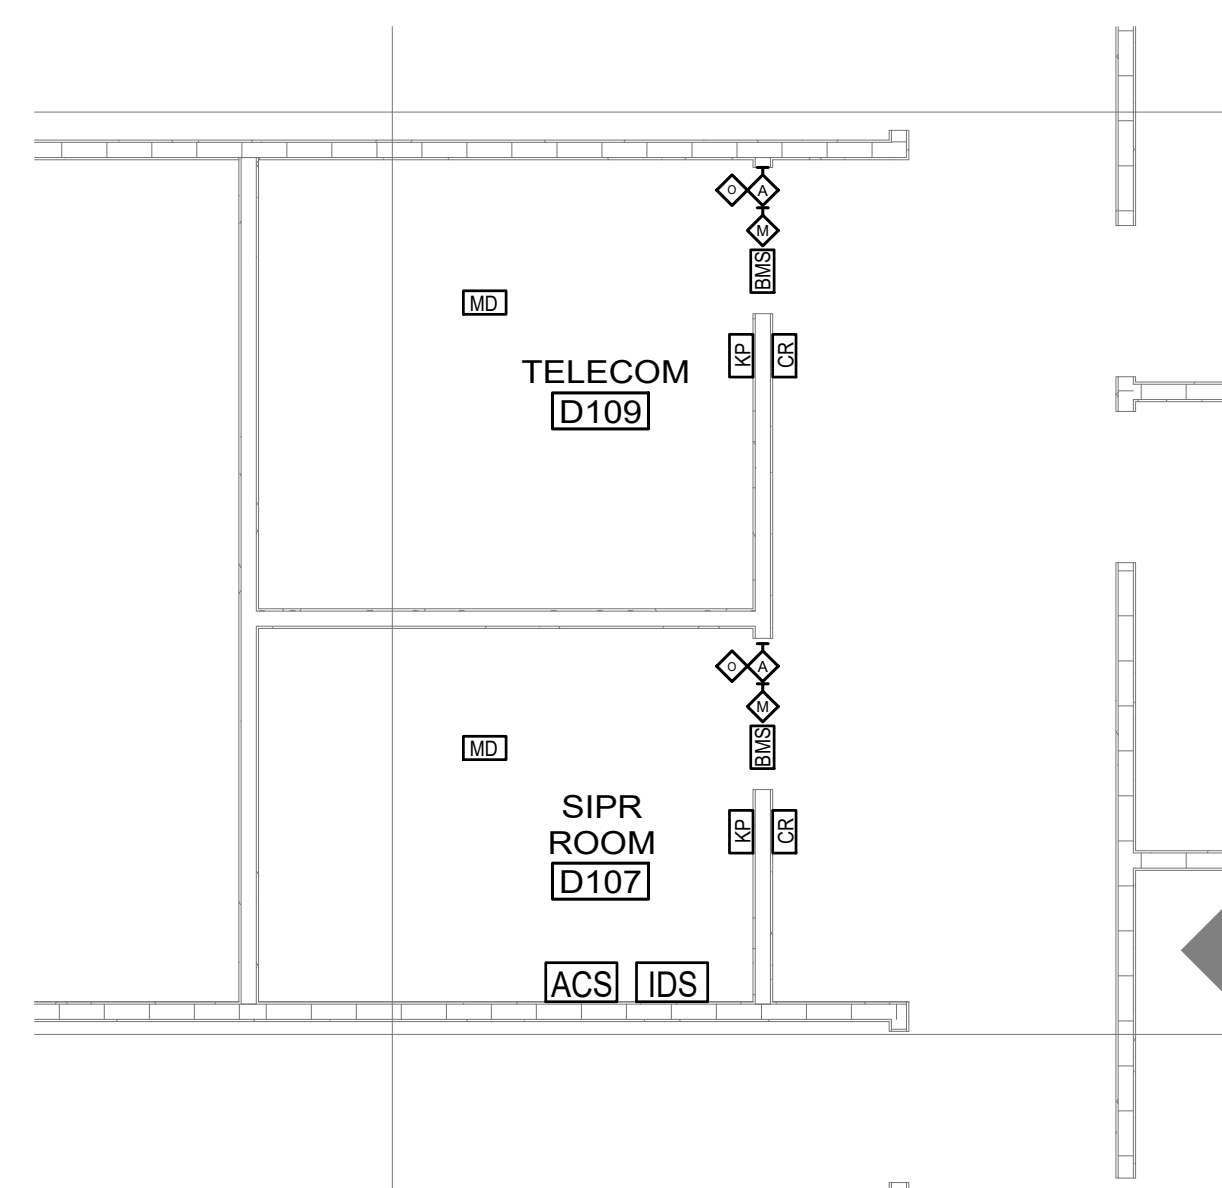

J4 SSAW - ENLARGED SECURITY PLAN

<u>ACCESS CONTROL SYSTEM (ACS)</u>	
	ACCESS CONTROL PANEL
	ELECTRIFIED DOOR LOCK
	MAGNETIC DOOR POSITION SWITCH
	CARD READER
	MOTION SENSOR DOOR RELEASE

<u>INTRUSION DETECTION SYSTEM (IDS)</u>	
	INTRUSION DETECTION SYSTEM (IDS) PANEL
	IDS BALANCED MAGNETIC DOOR SWITCH
	IDS KEY PAD
	IDS PASSIVE INFRARED MOTION SENSOR, DOWN VIEW
	IDS PASSIVE INFRARED MOTION SENSOR, 360 VIEW

GENERAL NOTES

US Army Corps
of Engineers®[illegible]

US ARMY CORPS OF ENGINEERS JAPAN DISTRICT, OKINAWA AREA OFFICE USARPJ-1 UNIT 35132 APO, AP 96374-5132		DESIGNED BY: DRAWN BY: CHECKED BY: SUBMITTED BY: SIZE:	ISSUE DATE: SOLICITATION NO.: CONTRACT NO.: SCALE: AS SHOWN FILE NAME:
 SSPM INTERNATIONAL, INC. 501 SUMMER STREET, SUITE 620			


KADENA AIR BASE, OKINAWA, JAPAN
VEHICLE MAINTENANCE SHOP
FY20 MCA PN77833

SHEET ID
TYD40

INTERMEDIATE DESIGN

CLIN 0004

KEY PLAN

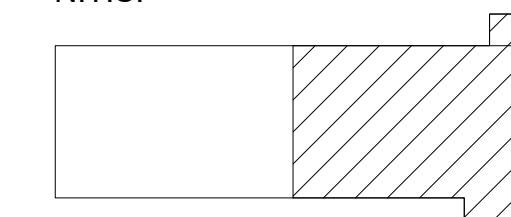SSAW
N.T.S.


GRAPHIC SCALE



SCALE: 1 : 50




ALL DIMENSIONS AND/OR DIMENSIONS SHOWN IN
CALLOUT/ NOTES ARE IN MILLIMETERS UNLESS
OTHERWISE NOTED.

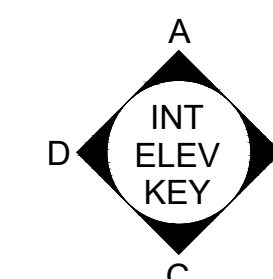


— O —
 — N —
 — M —
 — L —
 — K —
 — J —
 — I —
 — H —
 — G —
 — F —
 — E —
 — D —
 — C —
 — B —
 — A —

IDS NOTES:

1. IDS SYSTEM SHALL BE INSTALLED IN ACCORDANCE WITH ICD 705 AND BE ABLE TO COMMUNICATE WITH BLDG 705 / 18 SECURITY OFFICE. TYPES OF SENSORS AND MOTION DETECTORS ARE LISTED IN THE ICD-705.
2. THE CONTRACTOR SHALL BE RESPONSIBLE TO VERIFY THE PROPER DEVICE COVERAGE FOR THE PROTECTED SPACES.
3. ALL IDS SYSTEMS SHALL BE THE SAME MANUFACTURE AND SHOULD BE A COMPLETE FUNCTIONAL SYSTEM, INCLUDE DEVICES, CONTROL PANELS AND WIRING PROVIDED BY THE CONTRACTOR.
4. IDS INSTALLER SHOULD BE UL2050 CERTIFIED AND THEY SHALL FOLLOW ICD 705 AND UL 634.

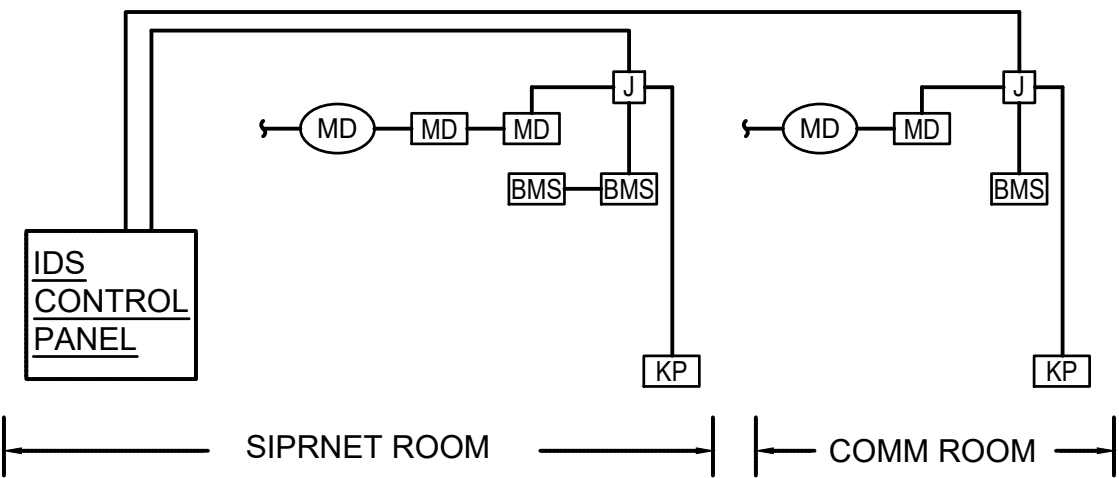

G1 IDS RISER DIAGRAM

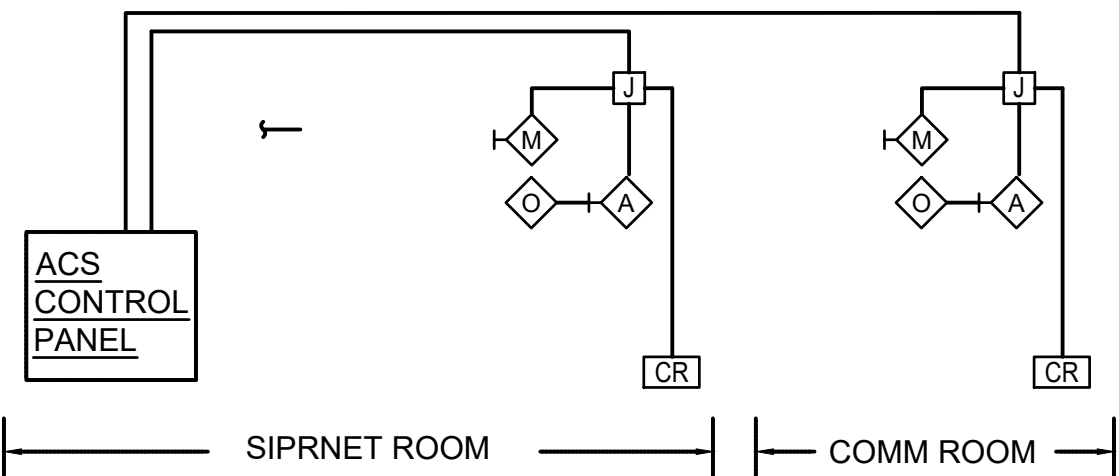

B1 ACS RISER DIAGRAM

CLIN 0004



US Army Corps
of Engineers®

[illegible]

 SSFP INTERNATIONAL SSFP INTERNATIONAL 507 SILVERSTONE STREET, SUITE 620 HONOLULU, HAWAII 96817	DESIGNED BY:	ISSUE DATE:
	DRAWN BY:	SOLICITATION NO.:
	CHECKED BY:	CONTRACT NO.:
	SUBMITTED BY:	SCALE:
	FILE NAME:	AS SHOWN
	SIZE:	
	ISO A1	

KADENA AIR BASE, OKINAWA, JAPAN
VEHICLE MAINTENANCE SHOP
FY20 MCA PN77833


SSAW - SECURITY RISER DIAGRAM (CLIN 0004)

SHEET ID

TYD601

INTERMEDIATE DESIGN


P
O
N
M
L
K
J
I
H
G
F
E
D
C
B
A

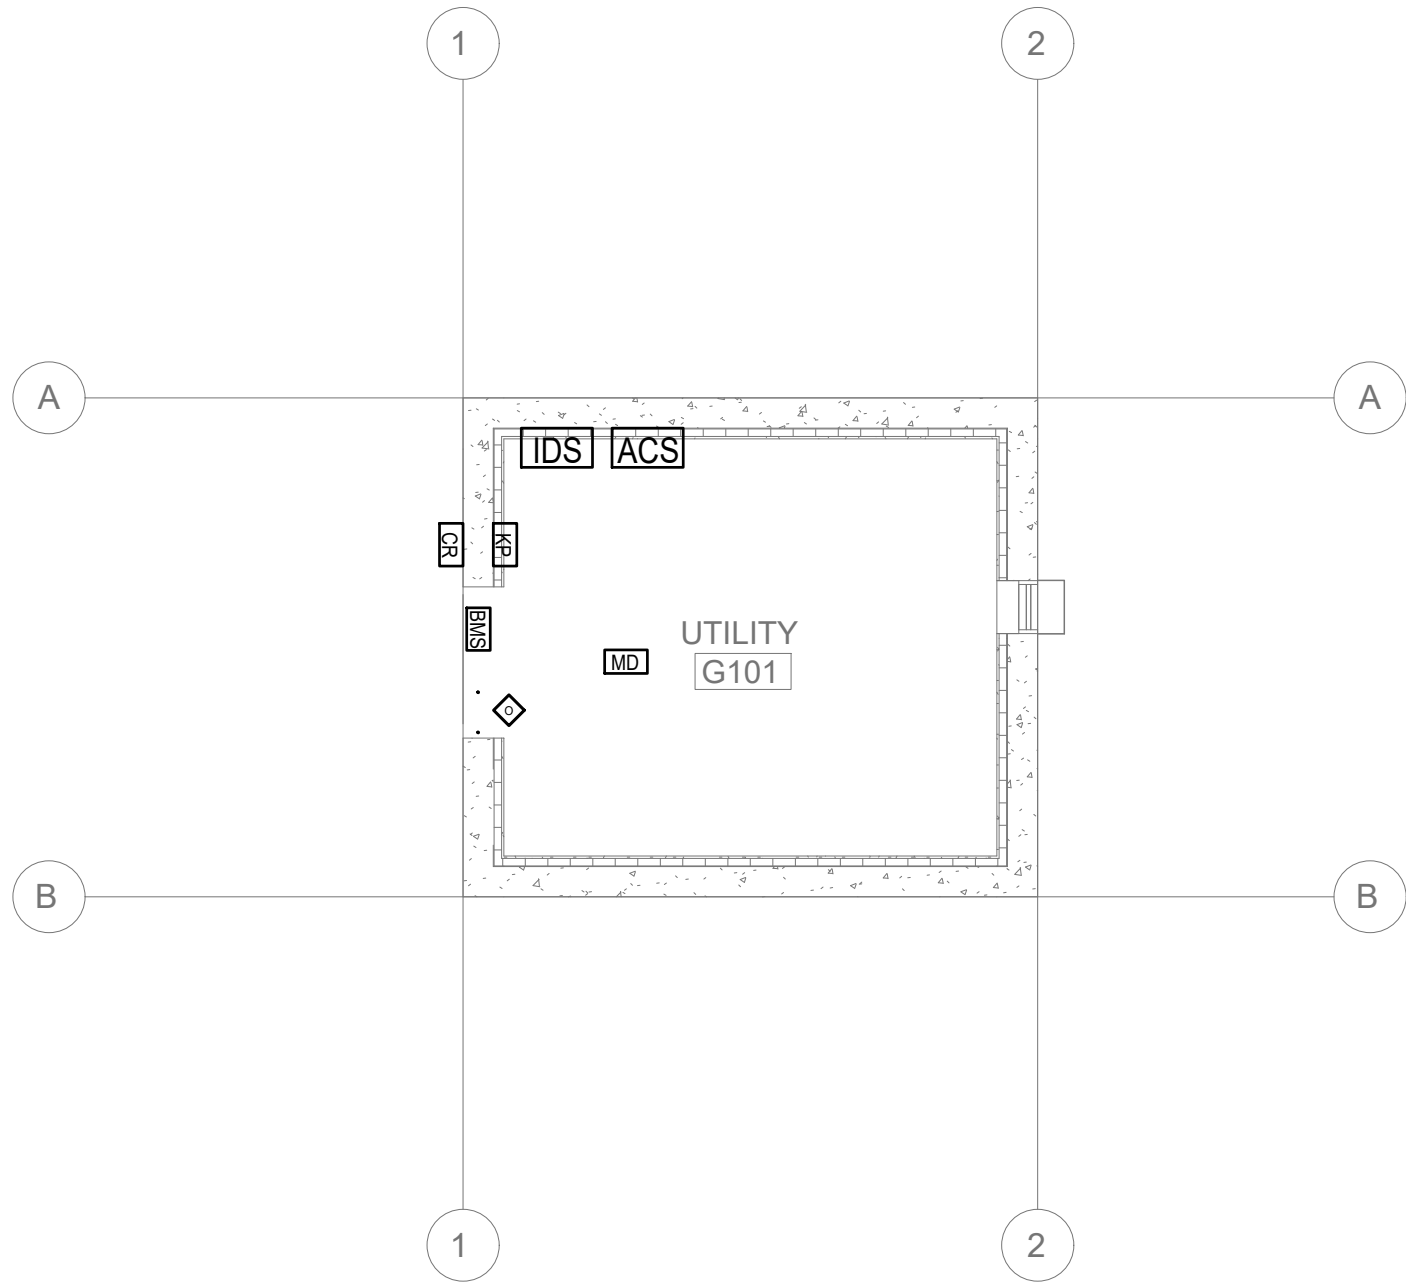

12 CH - SECURITY PLAN (CLIN 0001)
1:50

ACCESS CONTROL SYSTEM (ACS)	
ACP	ACCESS CONTROL PANEL
A	ELECTRIFIED DOOR LOCK
M	MAGNETIC DOOR POSITION SWITCH
CR	CARD READER
O	MOTION SENSOR DOOR RELEASE
INTRUSION DETECTION SYSTEM (IDS)	
IDS	INTRUSION DETECTION SYSTEM (IDS) PANEL
BMS	IDS BALANCED MAGNETIC DOOR SWITCH
KP	IDS KEY PAD
MD	IDS PASSIVE INFRARED MOTION SENSOR, DOWN VIEW
	IDS PASSIVE INFRARED MOTION SENSOR, 360 VIEW

GENERAL NOTES

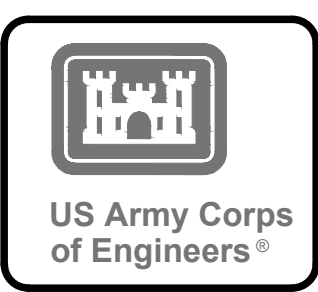

GENERAL NOTES - RCP


LEGEND

CLIN 0001


GRAPHIC SCALE



SCALE: 1 : 50

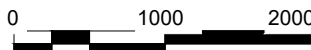

ALL DIMENSIONS AND/OR DIMENSIONS SHOWN IN
CALLOUT/ NOTES ARE IN MILLIMETERS UNLESS
OTHERWISE NOTED.

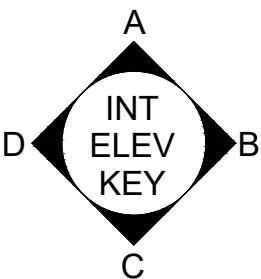

US ARMY CORPS OF ENGINEERS
JAPAN DISTRICT, OKINAWA AREA OFFICE
USAED-J UNIT 35132
APO, AP 96374-5132
SSEFM
SSEFM INTERNATIONAL, INC.
501 SUMNER STREET, SUITE 620
HONOLULU, HAWAII 96817

KADENA AIR BASE, OKINAWA, JAPAN
VEHICLE MAINTENANCE SHOP
FY20 MCA PN77833
CH - SECURITY PLANS (CLIN 0001)

SHEET ID


TYG101

INTERMEDIATE DESIGN


A — B — C — D — E — F — G — H — I — J — K — L — M — N — O — P —

IDS NOTES:

1. IDS SYSTEM SHALL BE INSTALLED IN ACCORDANCE WITH ICD 705 AND BE ABLE TO COMMUNICATE WITH BLDG 705 / 18 SECURITY OFFICE. TYPES OF SENSORS AND MOTION DETECTORS ARE LISTED IN THE ICD-705.
2. THE CONTRACTOR SHALL BE RESPONSIBLE TO VERIFY THE PROPER DEVICE COVERAGE FOR THE PROTECTED SPACES.
3. ALL IDS SYSTEMS SHALL BE THE SAME MANUFACTURE AND SHOULD BE A COMPLETE FUNCTIONAL SYSTEM, INCLUDE DEVICES, CONTROL PANELS AND WIRING PROVIDED BY THE CONTRACTOR.
4. IDS INSTALLER SHOULD BE UL2050 CERTIFIED AND THEY SHALL FOLLOW ICD 705 AND UL 634.

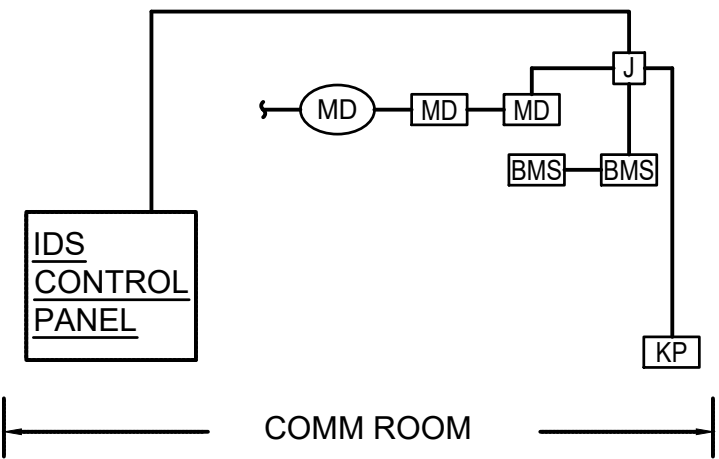

G1 IDS RISER DIAGRAM

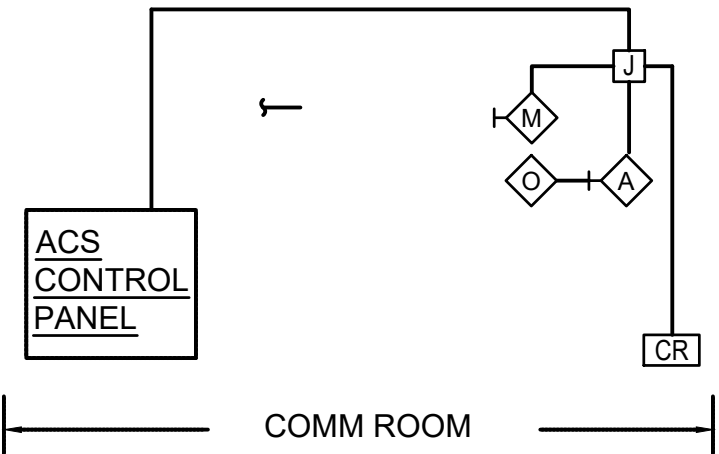

B1 ACS RISER DIAGRAM

CLIN 0001



US Army Corps
of Engineers®

[illegible]

 SSFP INTERNATIONAL SSFP INTERNATIONAL 507 SILVERSTONE STREET, SUITE 620 HONOLULU, HAWAII 96817	DESIGNED BY:	ISSUE DATE:
	DRAWN BY:	SOLICITATION NO.:
	CHECKED BY:	CONTRACT NO.:
	SUBMITTED BY:	SCALE:
	FILE NAME:	AS SHOWN
	SIZE:	
	ISO A1	

KADENA AIR BASE, OKINAWA, JAPAN
VEHICLE MAINTENANCE SHOP
FY20 MCA PN77833


SHEET ID

TYG601

INTERMEDIATE DESIGN

Architectural drawing of the 2nd floor security plan. The drawing shows a section of the floor with a large 'DRAFT' watermark. Key areas labeled include 'HALL H201' and 'WOMEN'S TOILET'. A legend table titled 'ACCESS CONTROL SYSTEM (ACS)' is located in the bottom right corner.

ACCESS CONTROL SYSTEM (ACS)	
	ACCESS CONTROL PANEL
	ELECTRIFIED DOOR LOCK
	MAGNETIC DOOR POSITION SWITCH
	CARD READER

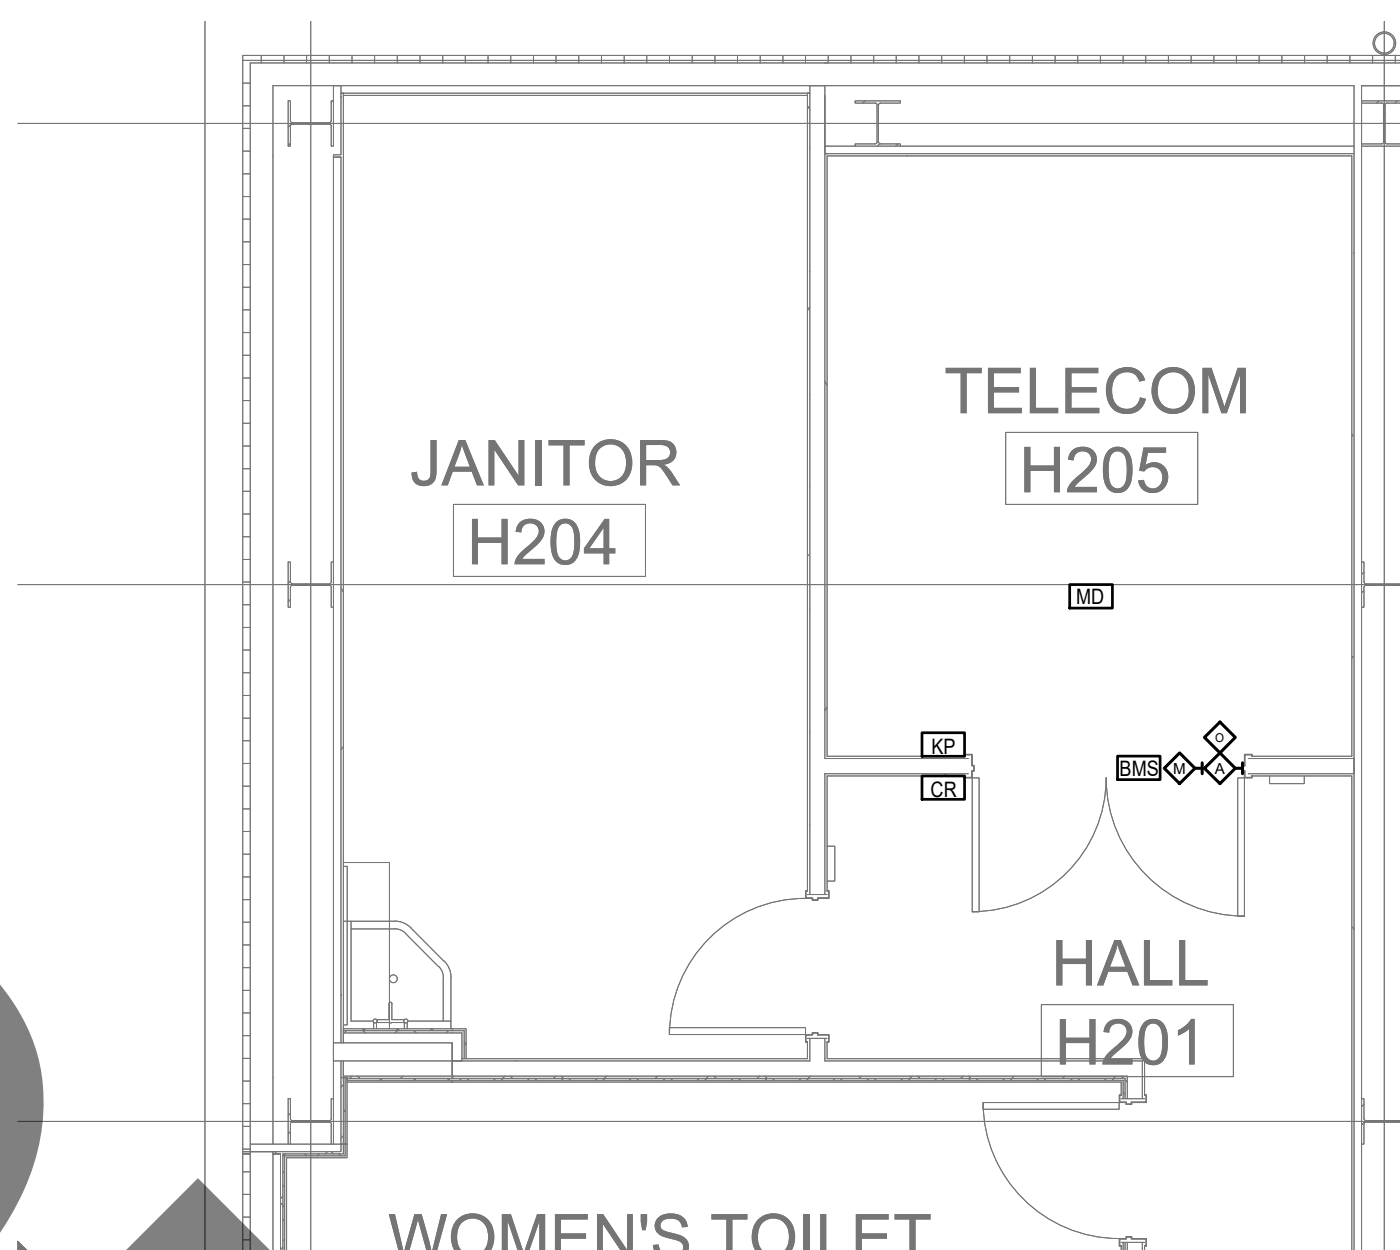


19 COF SS - ENLARGED 2ND FLOOR SECURITY PLAN
1:50

<u>ACCESS CONTROL SYSTEM (ACS)</u>	
	ACCESS CONTROL PANEL
	ELECTRIFIED DOOR LOCK
	MAGNETIC DOOR POSITION SWITCH
	CARD READER
	MOTION SENSOR DOOR RELEASE

<u>INTRUSION DETECTION SYSTEM (IDS)</u>	
	INTRUSION DETECTION SYSTEM (IDS) PANEL
	IDS BALANCED MAGNETIC DOOR SWITCH
	IDS KEY PAD
	IDS PASSIVE INFRARED MOTION SENSOR, DOWN VIEW
	IDS PASSIVE INFRARED MOTION SENSOR, 360 VIEW

CLIN 0004


GRAPHIC SCALE

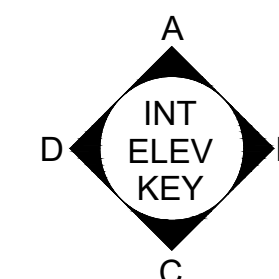

SCALE: 1 : 50

ALL DIMENSIONS AND/OR DIMENSIONS SHOWN IN
CALLOUT/ NOTES ARE IN MILLIMETERS UNLESS
OTHERWISE NOTED.

[illegible]

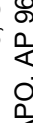US ARMY CORPS OF ENGINEERS JAPAN DISTRICT, OKINAWA AREA OFFICE USAE-D, JUNIT 35132 APO, APF 96374-5132	DESIGNED BY:	ISSUE DATE:
 SOFM INTERNATIONAL, INC. 501 SUMMER STREET, SUITE 620	DRAWN BY:	SOLICITATION NO.:
	CHECKED BY:	CONTRACT NO.:
	SUBMITTED BY:	SCALE: AS SHOWN
	SIZE:	FILE NAME:

KADENA AIR BASE, OKINAWA, JAPAN
VEHICLE MAINTENANCE SHOP
FY20 MCA PN77833

COF SS - ENLARGED PLANS (CLIN 0004)

SHEET ID

TYH401


INTERMEDIATE DESIGN

DRAFT

1. IDS SYSTEM SHALL BE INSTALLED IN ACCORDANCE WITH ICD 705 AND BE ABLE TO COMMUNICATE WITH BLDG 705 / 18 SECURITY OFFICE. TYPES OF SENSORS AND MOTION DETECTORS ARE LISTED IN THE ICD-705.
2. THE CONTRACTOR SHALL BE RESPONSIBLE TO VERIFY THE PROPER DEVICE COVERAGE FOR THE PROTECTED SPACES.
3. ALL IDS SYSTEMS SHALL BE THE SAME MANUFACTURE AND SHOULD BE A COMPLETE FUNCTIONAL SYSTEM, INCLUDE DEVICES, CONTROL PANELS AND WIRING PROVIDED BY THE CONTRACTOR.
4. IDS INSTALLER SHOULD BE UL2050 CERTIFIED AND THEY SHALL FOLLOW ICD 705 AND UL 634.



CLIN 0004

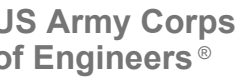[illegible]

 SSPM INTERNATIONAL 507 SUMNER STREET, SUITE 620 HONOLULU, HAWAII 96817	DESIGNED BY:	ISSUE DATE:
	DRAWN BY:	SOLICITATION NO.:
	CHECKED BY:	CONTRACT NO.:
	SUBMITTED BY:	SCALE: AS SHOWN
	SIZE: ISO A1	FILE NAME:


KADENA AIR BASE, OKINAWA, JAPAN
VEHICLE MAINTENANCE SHOP
FY20 MCA PN77833

SHEET ID


TYH601

INTERMEDIATE DESIGN


A — B — C — D — E — F — G — H — I — J — K — L — M — N — O — P

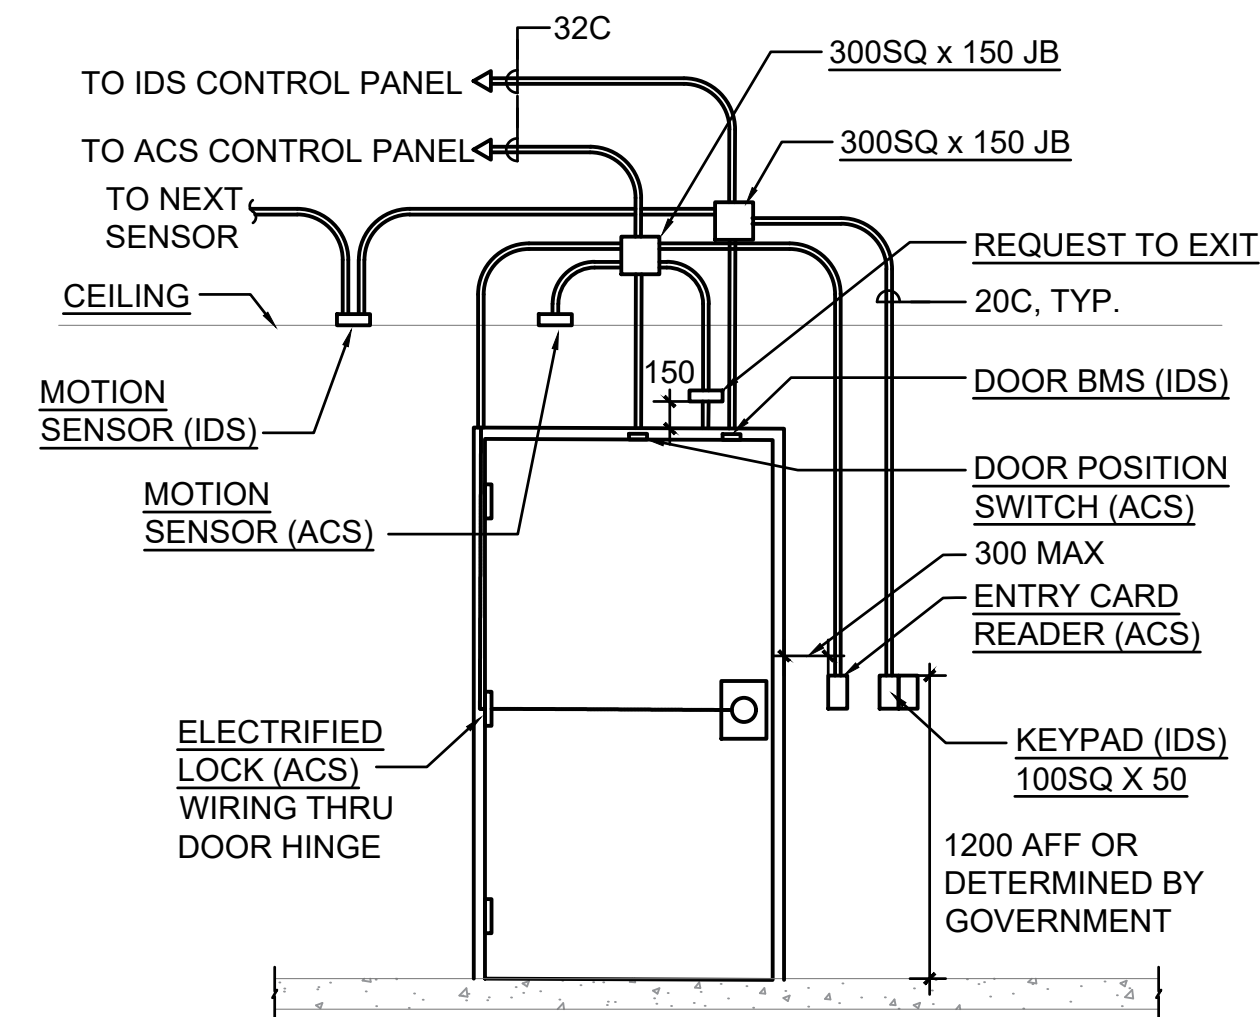

J3 DOOR ELEVATION (IDS & ACS)
NONE

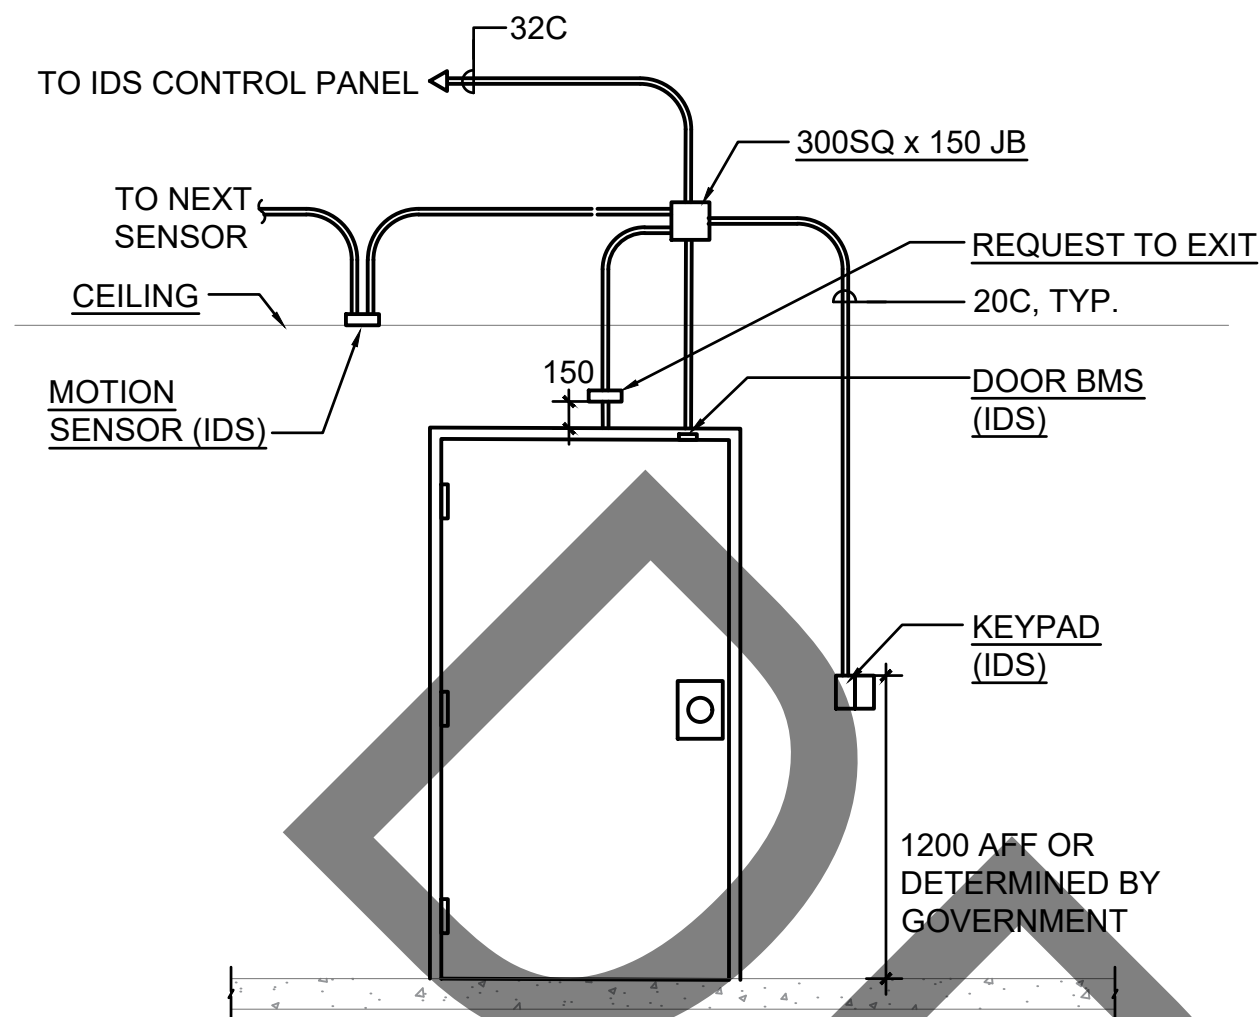

J8 DOOR ELEVATION (IDS ONLY)
NONE

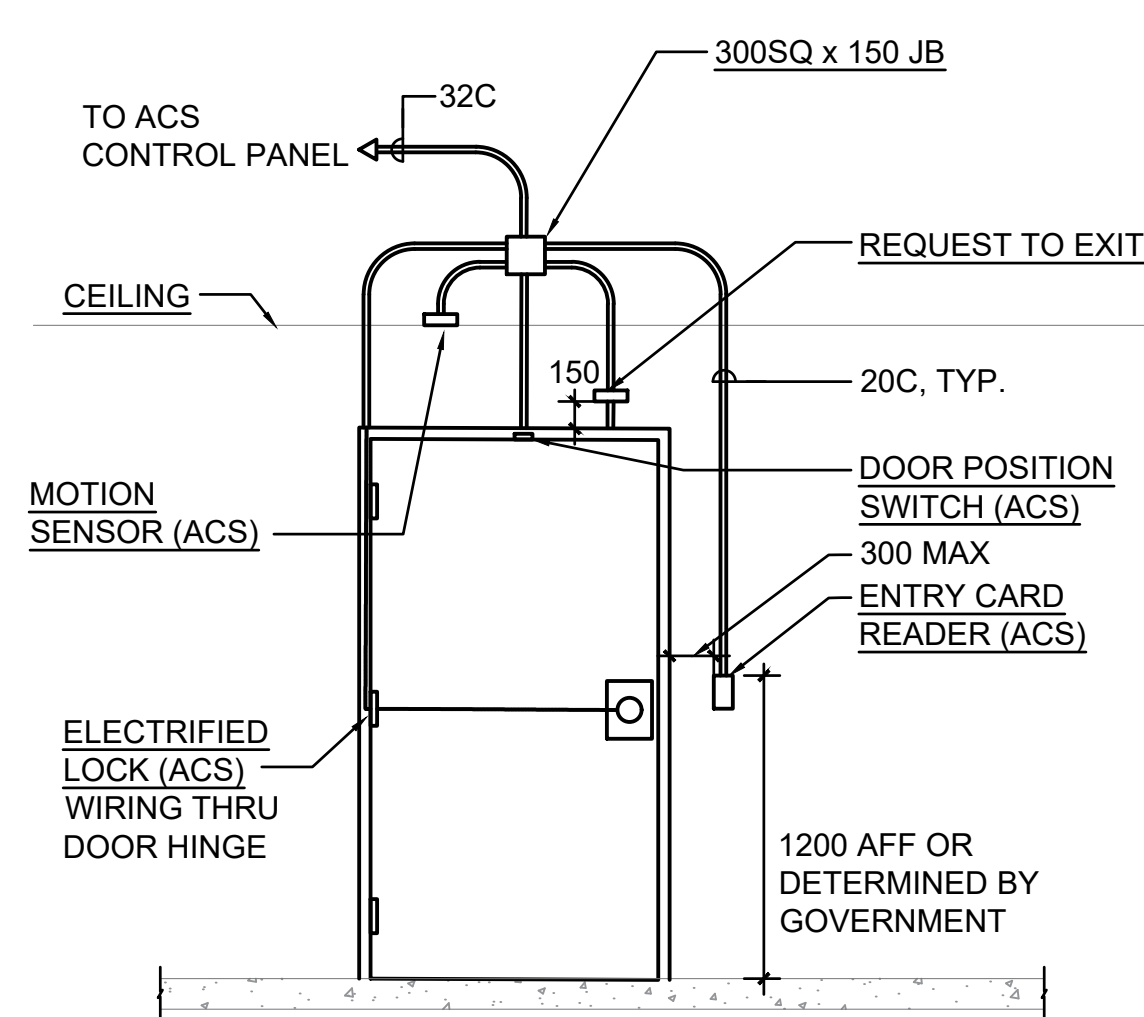

J13 DOOR ELEVATION (ACS ONLY)
NONE



US Army Corps
of Engineers®

Item	Quantity	Unit	Price	Total
1. 1000	1000	kg	1000	1000
2. 1000	1000	kg	1000	1000
70. 1000	1000	kg	1000	

US ARMY CORPS OF ENGINEERS JAPAN DISTRICT, OKINAWA AREA OFFICE U.S. ARMY BOX 392 APO, APF 96374-392	DESIGNED BY: DRAWN BY: CHECKED BY: SUBMITTED BY: SIZE:	ISSUE DATE: SOLICITATION NO.: CONTRACT NO.: SCALE: AS SHOWN FILE NAME:
 S&P INTERNATIONAL, INC 5501 SUMNER STREET, SUITE 620		

KADENA AIR BASE, OKINAWA, JAPAN
VEHICLE MAINTENANCE SHOP
F120 MCA PN77835

SECURITY SYSTEM DETAILS

SHEET ID

TY501

INTERMEDIATE DESIGN

1. THE ENTIRE SYSTEM MUST COMPLY WITH ALL APPLICABLE REQUIREMENTS OF THE MILITARY HANDBOOKS, MILITARY ENGINEERING TECHNICAL LETTERS, INTERNATIONAL BUILDING CODE, INTERNATIONAL PLUMBING CODE, AND AGENCIES HAVING JURISDICTION.
2. THE DRAWINGS AND SPECIFICATIONS ARE INTENDED TO COVER THE COMPLETE INSTALLATION OF SYSTEMS TO FUNCTION AS DESCRIBED AND SPECIFIED. THE OMISSION OF REFERENCE TO ANY NECESSARY ITEM OF LABOR OR MATERIAL SHALL NOT RELIEVE THE CONTRACTOR FROM PROVIDING SUCH LABOR AND MATERIAL.
3. PROVIDE EQUIPMENT CAPABLE OF FITTING INTO THE SPACES ALLOCATED WHILE MEETING THE MANUFACTURER'S RECOMMENDED ACCESS REQUIREMENTS. REVIEW ALL SPACES WHERE EQUIPMENT IS TO BE INSTALLED PRIOR TO ORDERING OF EQUIPMENT AND NOTIFY THE CONTRACTING OFFICER OF ANY INADEQUATE CLEARANCES OR CONDITIONS THAT WILL PREVENT THE PROPER INSTALLATION, MAINTENANCE, AND OPERATION OF THE EQUIPMENT.
4. COORDINATE WITH OTHER SYSTEMS PRIOR TO COMMENCING AND DURING CONSTRUCTION. OVERLAY PLANS AND RESOLVE ANY DISCREPANCIES OR CONFLICTS WITH OTHER SYSTEMS INCLUDING CLEAR SPACE AND SERVICEABILITY REQUIREMENTS.
5. VERIFY AND COORDINATE ALL ROOF, WALL AND FLOOR PENETRATIONS WITH THE STRUCTURAL AND ARCHITECTURAL DRAWINGS AND NOTIFY THE CONTRACTING OFFICER OF ANY CONFLICTS PRIOR TO START OF CONSTRUCTION.
6. OBTAIN APPROVAL FROM THE CONTRACTING OFFICER BEFORE MAKING ANY PENETRATIONS THROUGH STRUCTURAL MEMBERS, WALLS AND SLABS NOT INDICATED IN THE STRUCTURAL DRAWINGS.
7. VERIFY THE EXACT LOCATION, SIZE, AND INVERT OF ALL EXISTING SEWER, AND WATER LINES AT THE POINT OF CONNECTION PRIOR TO THE START OF CONSTRUCTION.
8. DRAWINGS DO NOT SHOW EXACT DETAILS OF PIPING. PROVIDE OFFSETS AS NECESSARY TO AVOID LOCAL OBSTRUCTIONS OR INTERFERENCE WITH OTHER SYSTEMS. REVIEW ALL PIPING AND DUCT RUNS PRIOR TO FABRICATION AND IMMEDIATELY NOTIFY THE CONTRACTING OFFICER OF ANY INTERFERENCE AND/OR LACK OF ADEQUATE CLEARANCES.
9. SHOULD PROJECT CONDITIONS REQUIRE REARRANGEMENT OF WORK, MARK SUCH CHANGES ON THE AS-BUILT DRAWINGS AND NOTIFY THE CONTRACTING OFFICER. IF THESE CHANGES REQUIRE ALTERNATE METHODS TO THOSE APPROVED BY THE CONTRACT DOCUMENTS, SUBMIT SHOP DRAWINGS SHOWING THE PROPOSED ALTERNATE METHODS TO THE CONTRACTING OFFICER FOR REVIEW. DO NOT PROCEED UNTIL REVIEWED.
10. PATCH AND PAINT ALL EXPOSED MATERIAL, INCLUDING PIPING, TO MATCH ADJACENT SURFACES OR AS INDICATED.
11. FIRE STOP ALL PENETRATIONS THROUGH FIRE RATED WALLS, FLOORS, OR PARTITIONS WITH A UL APPROVED SYSTEM APPROPRIATE FOR THE PENETRATION TYPE AND FIRE RATING IN ACCORDANCE WITH MANUFACTURER'S INSTALLATION INSTRUCTIONS.
12. SEISMICALLY BRACE ALL EQUIPMENT AND PIPING FOR SEISMIC ZONE 4. BRACE SYSTEMS IN ACCORDANCE WITH SMACNA STANDARDS.
13. EXCLUDING BELOW GRADE PIPING, INSULATE ALL SEWER PIPING RECEIVING AIR CONDITIONING CONDENSATE DRAINS, OR ANY OTHER COLD LIQUID WHICH MAY CREATE CONDENSATION, FROM POINT OF CONNECTION TO MAIN SANITARY RISER.
14. PROVIDE WALL CLEANOUTS AT THE BASE OF ALL WASTE RISERS, UNLESS NOTED OTHERWISE.
15. PROVIDE COPPER LABELS INDICATING TYPE AND DIRECTIONAL FLOW TO THE PIPING.
16. PROVIDE ACCESS PANELS TO ALL VALVES, WATER HAMMER ARRESTERS, ETC. WHERE REQUIRED FOR SERVICE OR RESET. SIZE AND LOCATE PANELS PER MANUFACTURERS RECOMMENDATION AND FUTURE SERVICEABILITY.
17. SLOPE SANITARY SEWER 1% FOR ALL SANITARY PIPES 100MM AND ABOVE UNLESS NOTED OTHERWISE. SLOPE SANITARY SEWER 2% FOR ALL SANITARY PIPES BELOW 100MM UNLESS NOTED OTHERWISE.

SYMBOL	ABBREV.	DESCRIPTION
	AD	AREA DRAIN
	AF	ANTI-FREEZE
	BV	FLOW BALANCING VALVE
	DBP	BOOSTER PUMP
	CA	COMPRESSED AIR
	CO	CLEANOUT
	CONN.	CONNECTION
	COTG	CLEANOUT TO GRADE
	CW	COLD WATER
	CD	CONDENSATE DRAIN
		DUPLEX BASKET STRAINER
	EEWS	EMERGENCY EYEWASH SHOWER
	EO	ENGINE OIL
	ETP	ELECTRICAL TRAP PRIMER
	EWC	ELECTRIC WATER COOLER
	FCO	FLOOR CLEANOUT / CLEANOUT TO GRADE
	FD	FLOOR DRAIN
	FSK	FLOOR SINK
	GO	GEAR OIL
	GR	GREASE
	HB	HOSE BIBB
	HT	HOLDING TANK
	HW	HOT WATER
	HWR	HOT WATER RETURN
	INV	INVERT
	KS	KITCHEN SINK
	LAV	LAVATORY
	M	METER
	MM	MILIMETER
	MS	MOP SINK
	POC	POINT OF CONNECTION
	PRV	PRESSURE REGULATING VALVE
	RAD	RADON
	RM	ROOM
	RPBFP	REDUCED PRESSURE BACKFLOW PREVENTER
	S	SANITARY
	SH	SHOWER
	SD	STORM DRAIN
	SK	SINK
	T	TEMPERATURE SENSOR
	TD	TRENCH DRAIN
	TF	TRANSMISSION FLUID
	TP	TRAP PRIMER
	TYP	TYPICAL
	U/G	UNDERGROUND
	UR	URINAL
	V	VENT
	VTR	VENT THRU ROOF
	WCO	WALL CLEANOUT
	WMB	WASHING MACHINE BOX
	WC	WATER CLOSET
	WHA	WATER HAMMER ARRESTOR


[illegible]

DESIGNED BY: US ARMY CORPS OF ENGINEERS JAPAN ENGINEER DISTRICT OKINAWA AREA DISTRICT APO AP 96376-5152	DRAWN BY: I TSANG	SOLICITATION NO.:	ISSUE DATE:
DESIGN PARTNERS INCORPORATED 1580 MAKALOA STREET, SUITE 1100 HONOLULU, HAWAII 96814	CHECKED BY: O. CRAMER O. CRAMER	CONTRACT NO.: W912H1-7D-0003	AS SHOWN
	SIZE:	ANSI D	

APU AP 96343-5010
FY20 MCA PN77833 VEHICLE MAINTENANCE SHOP
GENERAL NOTES AND LEGEND

SHEET ID

P001

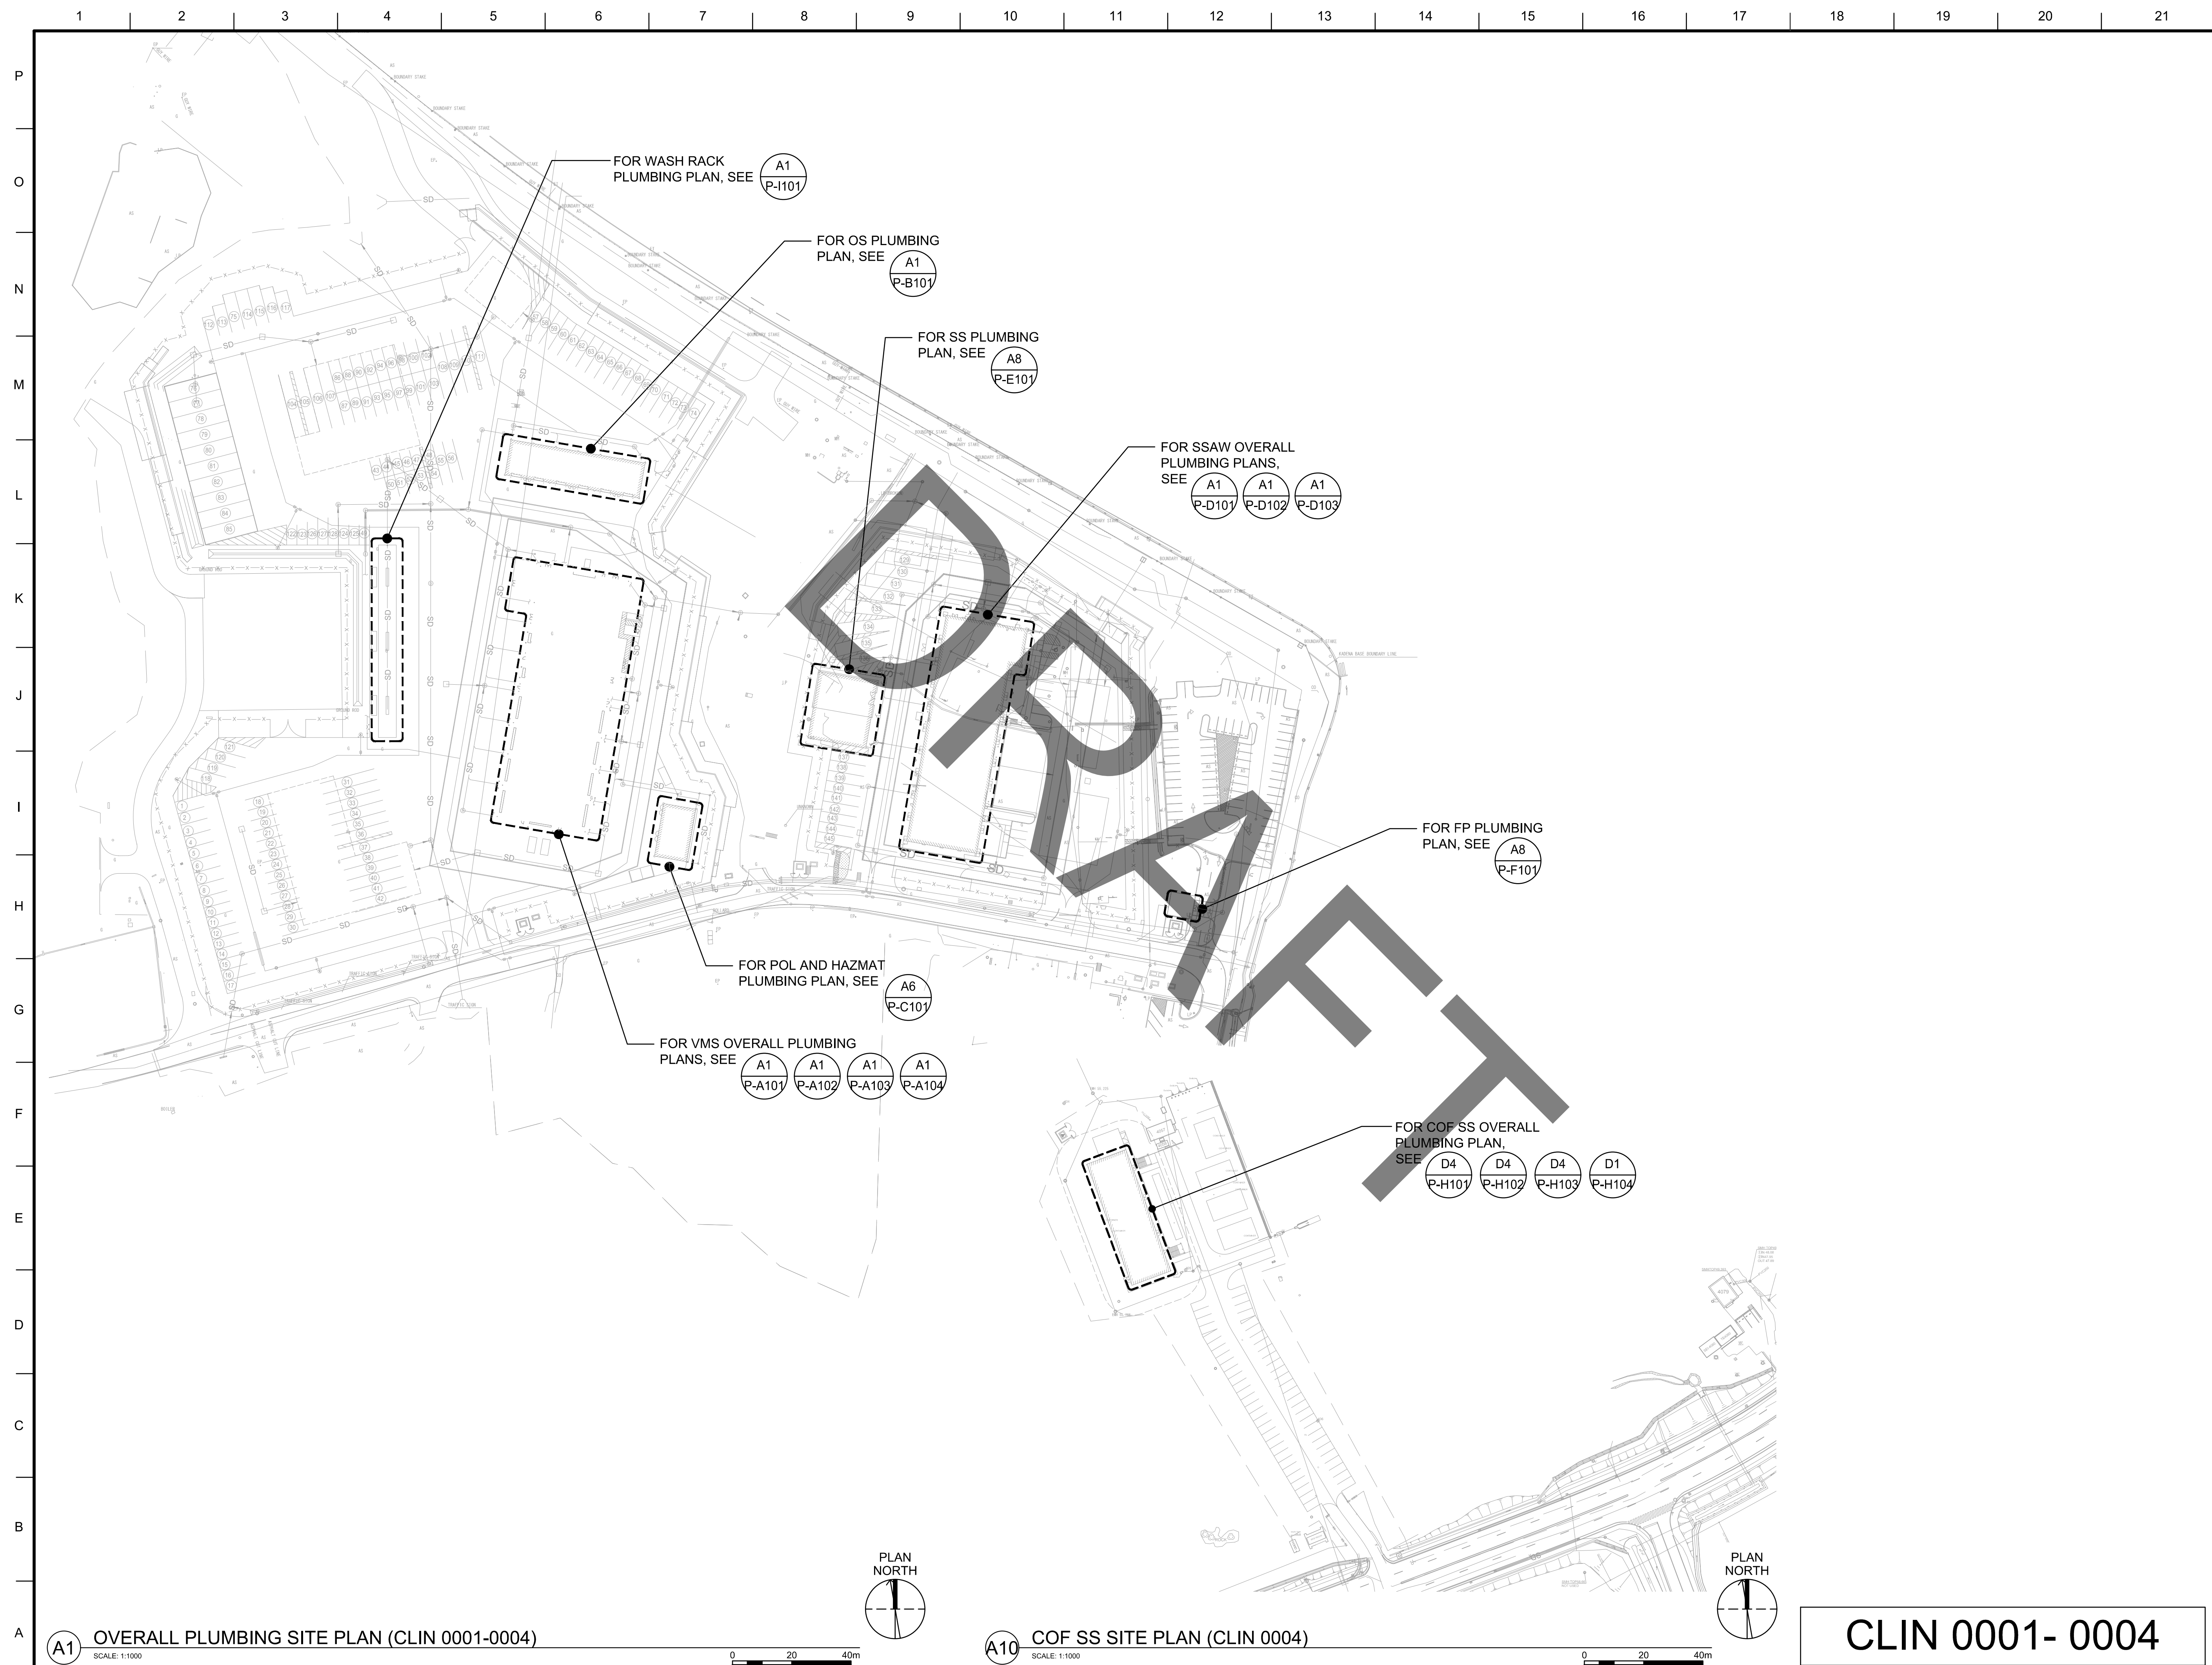US Army Corps
of Engineers®

--	--	

DESIGN PARTNERS INCORPORATED 1580 KALANIANAʻOHE BLVD, SUITE 100 HONOLULU, HAWAII 96814	DESIGNED BY: US ARMY CORPS OF ENGINEERS JAPAN ENGINEER DISTRICT OKINAWA AREA OFFICE APO AP 96376-5132	DRAWN BY: L TSANG	SOLICITATION NO.:	ISSUE DATE:
	CHECKED BY: 0. CRABTREE	CONTRACT NO.:		
	SUBMITTED BY: 0. CRABTREE	W912H-17-D-0003		
	SIZE: C	SCALE:	AS SHOWN	


APO AP 96343-5010
FY20 MCA PN77833 VEHICLE MAINTENANCE SHOP
OVERALL PLUMBING AND COF SS SITE PLAN (CLIN 00001-00004)


SHEET ID

P101


INTERMEDIATE DESIGN



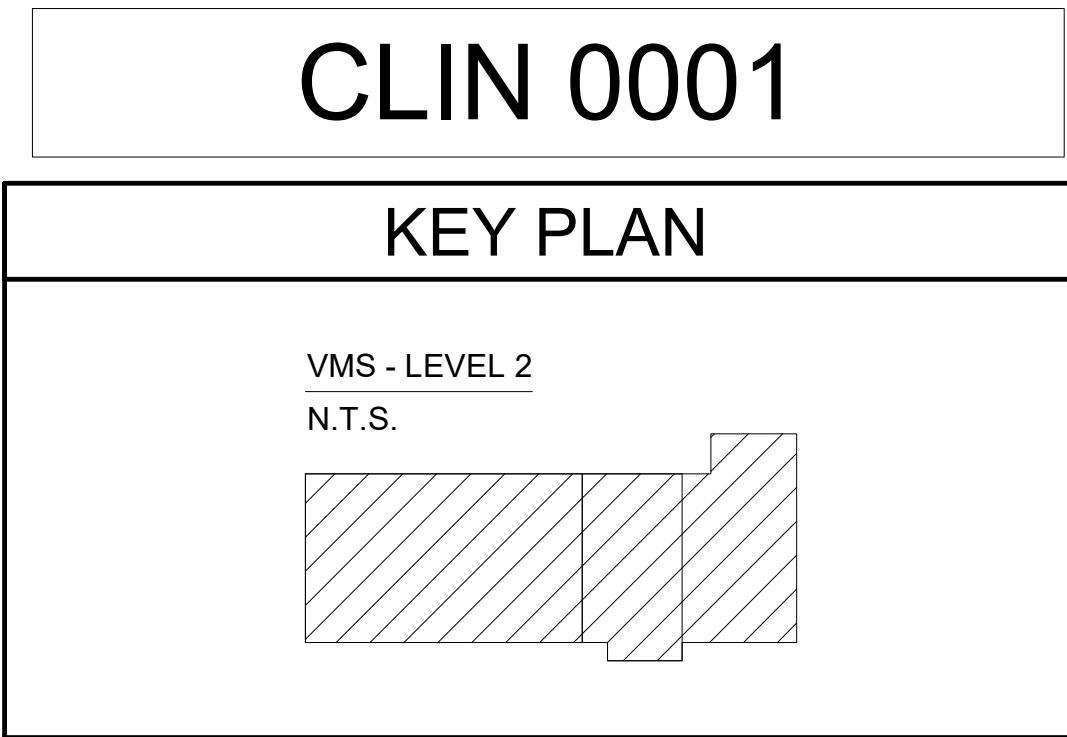

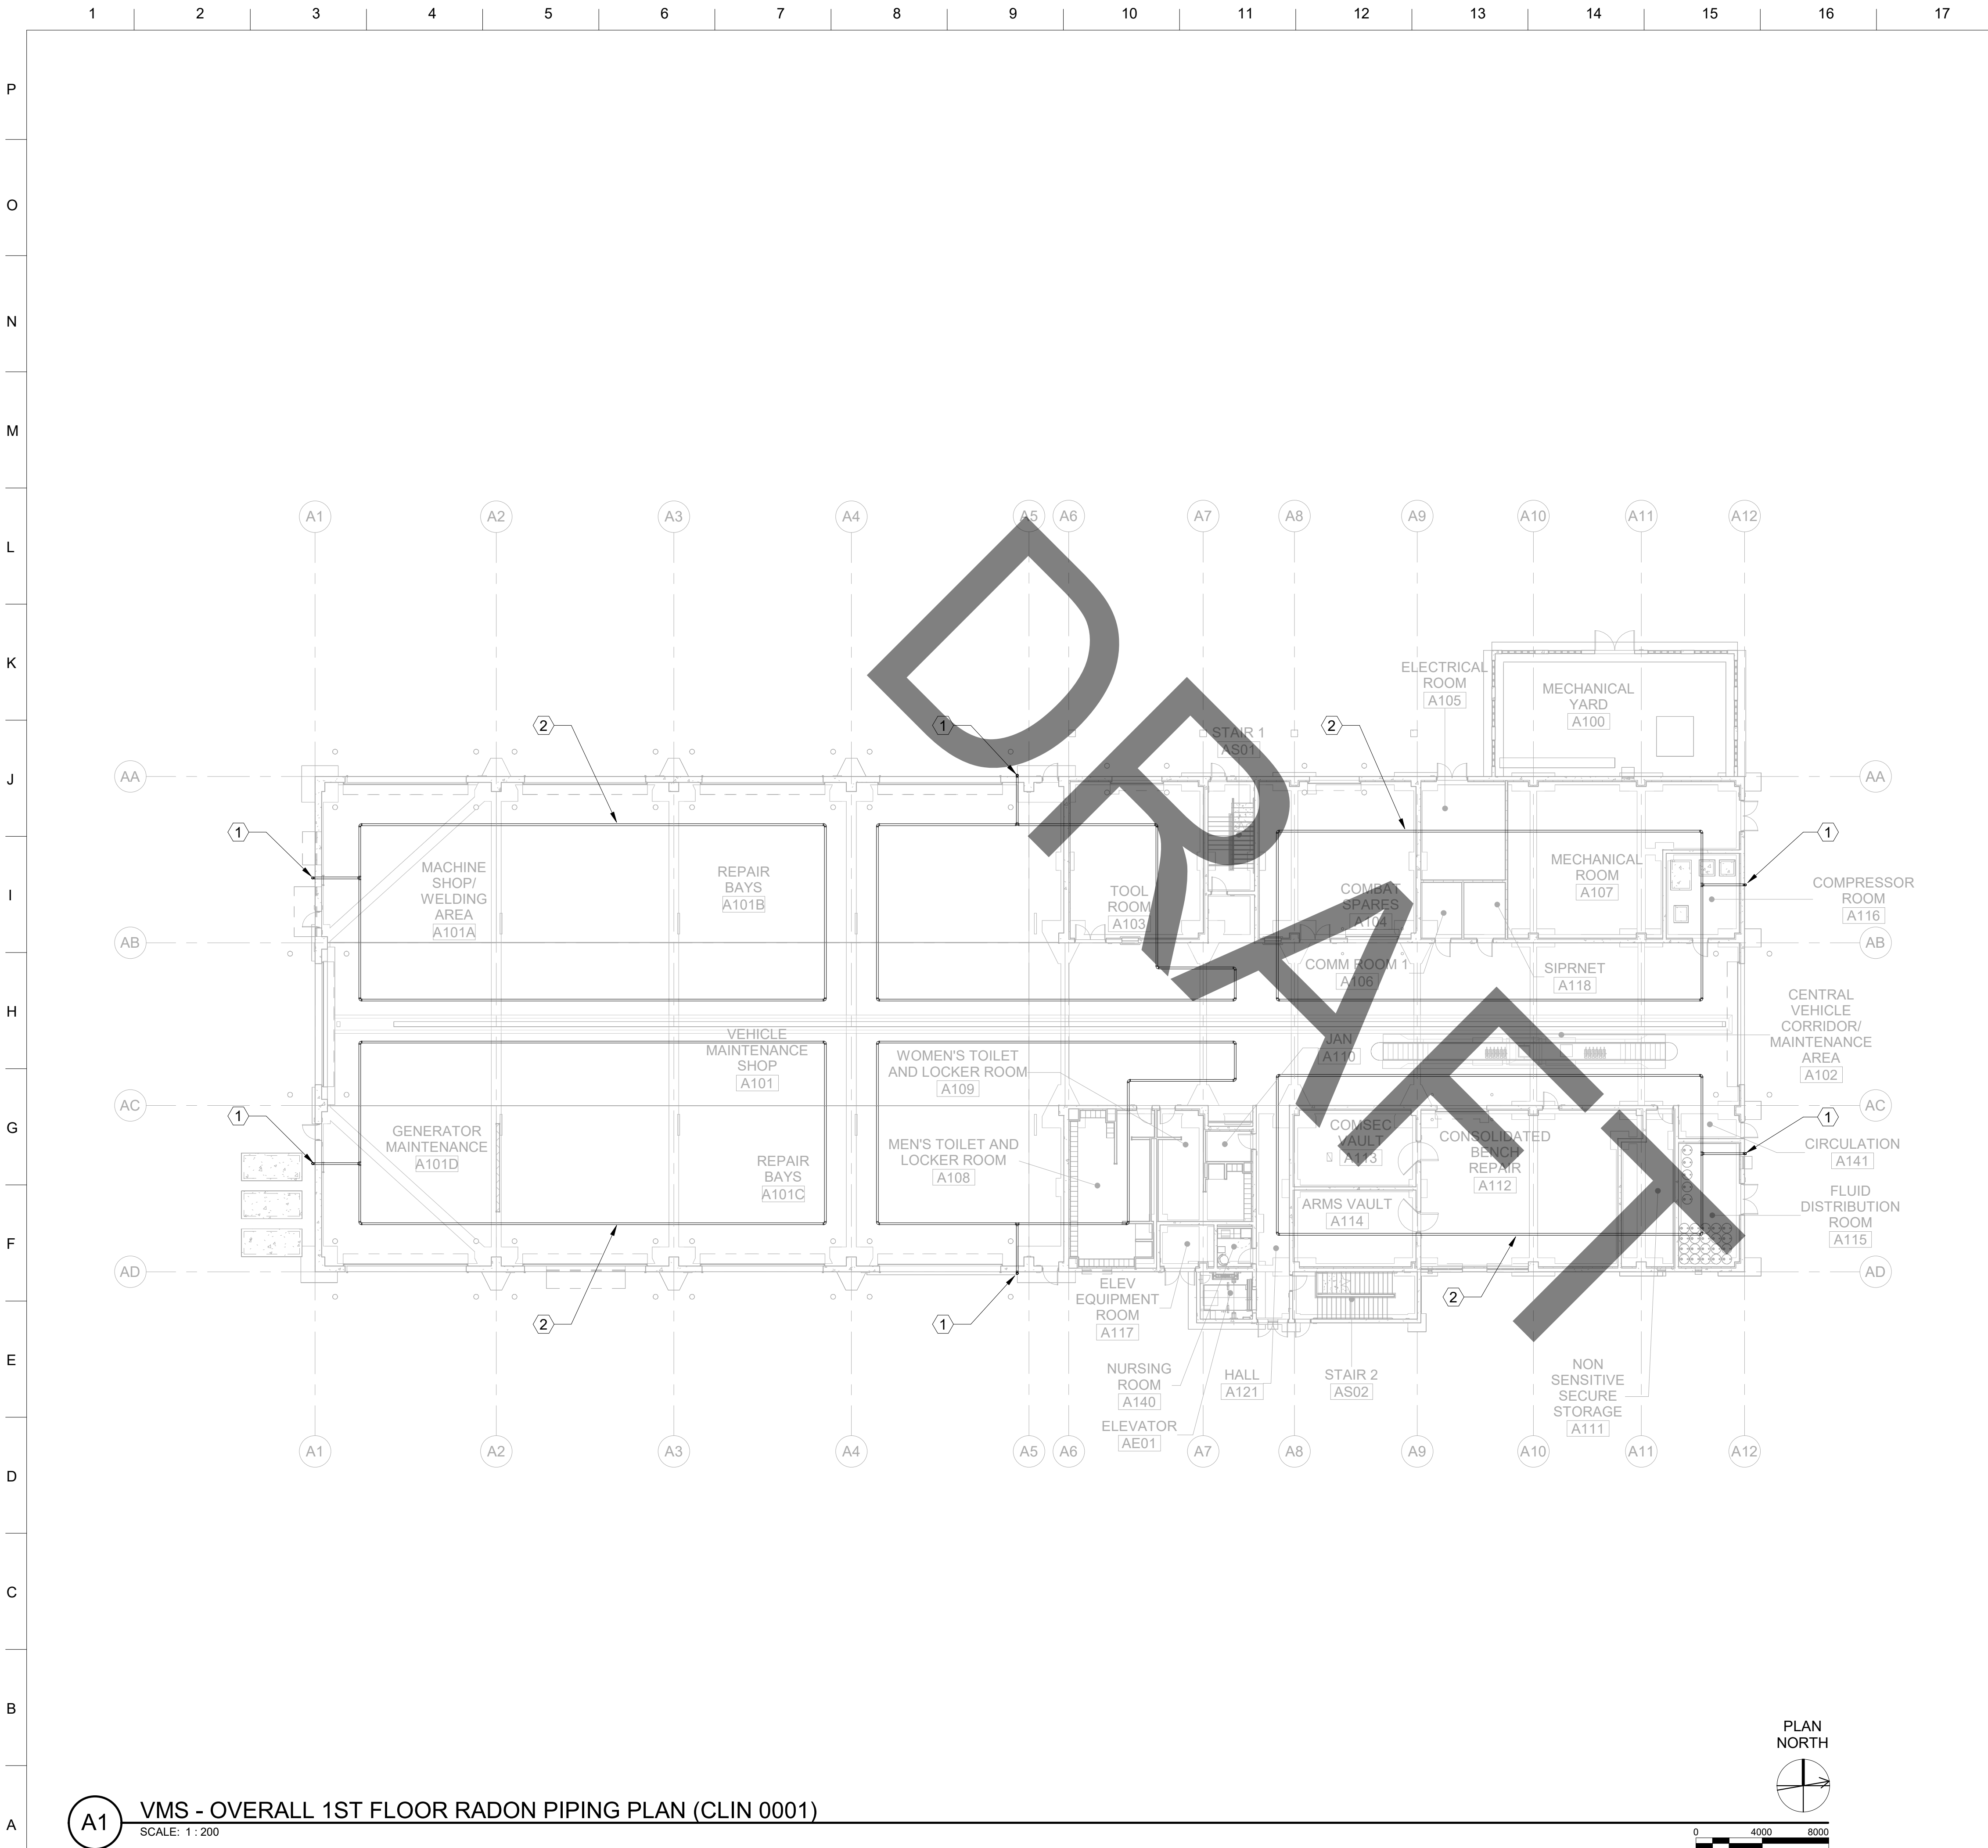


A1 VMS - OVERALL 1ST FLOOR RADON PIPING PLAN (CLIN 0001)
SCALE: 1 : 200

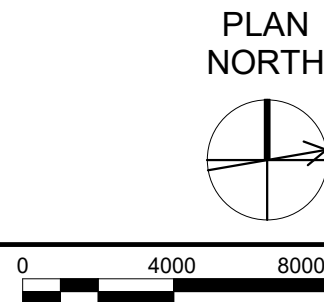

KEY NOTES

- 1 100MM RADON PIPING UP TO ROOF WITH SAMPLING BOX 1M ABOVE GRADE, TERMINATE PIPING 300MM ABOVE ROOF. ROUTE ALONG EXTERIOR OF BUILDING, PROVIDE ELECTRICAL OUTLETS FOR FUTURE RADON EXHAUST FANS MIN 1M ABOVE FINISHED GRADE, TYPICAL.
- 2 100MM PERFORATED RADON SOIL-GAS COLLECTION PIPE SYSTEM 300MM UNDER FLOOR SLAB AND 300MM FROM EXTERIOR WALL.

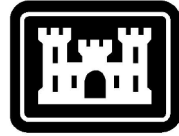

US Army Corps
of Engineers ®

MARK	DESCRIPTION	DATE

DESIGNED BY: I. TSANG	ISSUE DATE:
DRAWN BY: R. BALIGANSAY	SOLICITATION NO.:
CHECKED BY: W92AV-17-D-0003	CONTRACT NO.:
SUBMITTED BY:	SIZE: ANSI D
US ARMY CORPS OF ENGINEERS JAPAN ENGINEER DISTRICT OKINAWA AREA OFFICE APO AF 96376-5132	
DESIGN PARTNERS INCORPORATED 1580 MAKALOA STREET, SUITE 1100 HONOLULU, HAWAII 96814	

FY20 MCA PN7833 VEHICLE MAINTENANCE SHOP KADENA AIR BASE, OKINAWA, JAPAN	VMS - OVERALL 1ST FLOOR RADON PIPING PLAN (CLIN 0001)
---	--

SHEET ID

P-A103


INTERMEDIATE DESIGN

Plot Date: 12/15/2025 1:18:21 PM

File Path:

C:\Users\baligasa\Documents\51178_1TEMP_PUMP_2022_baligasa.rvt



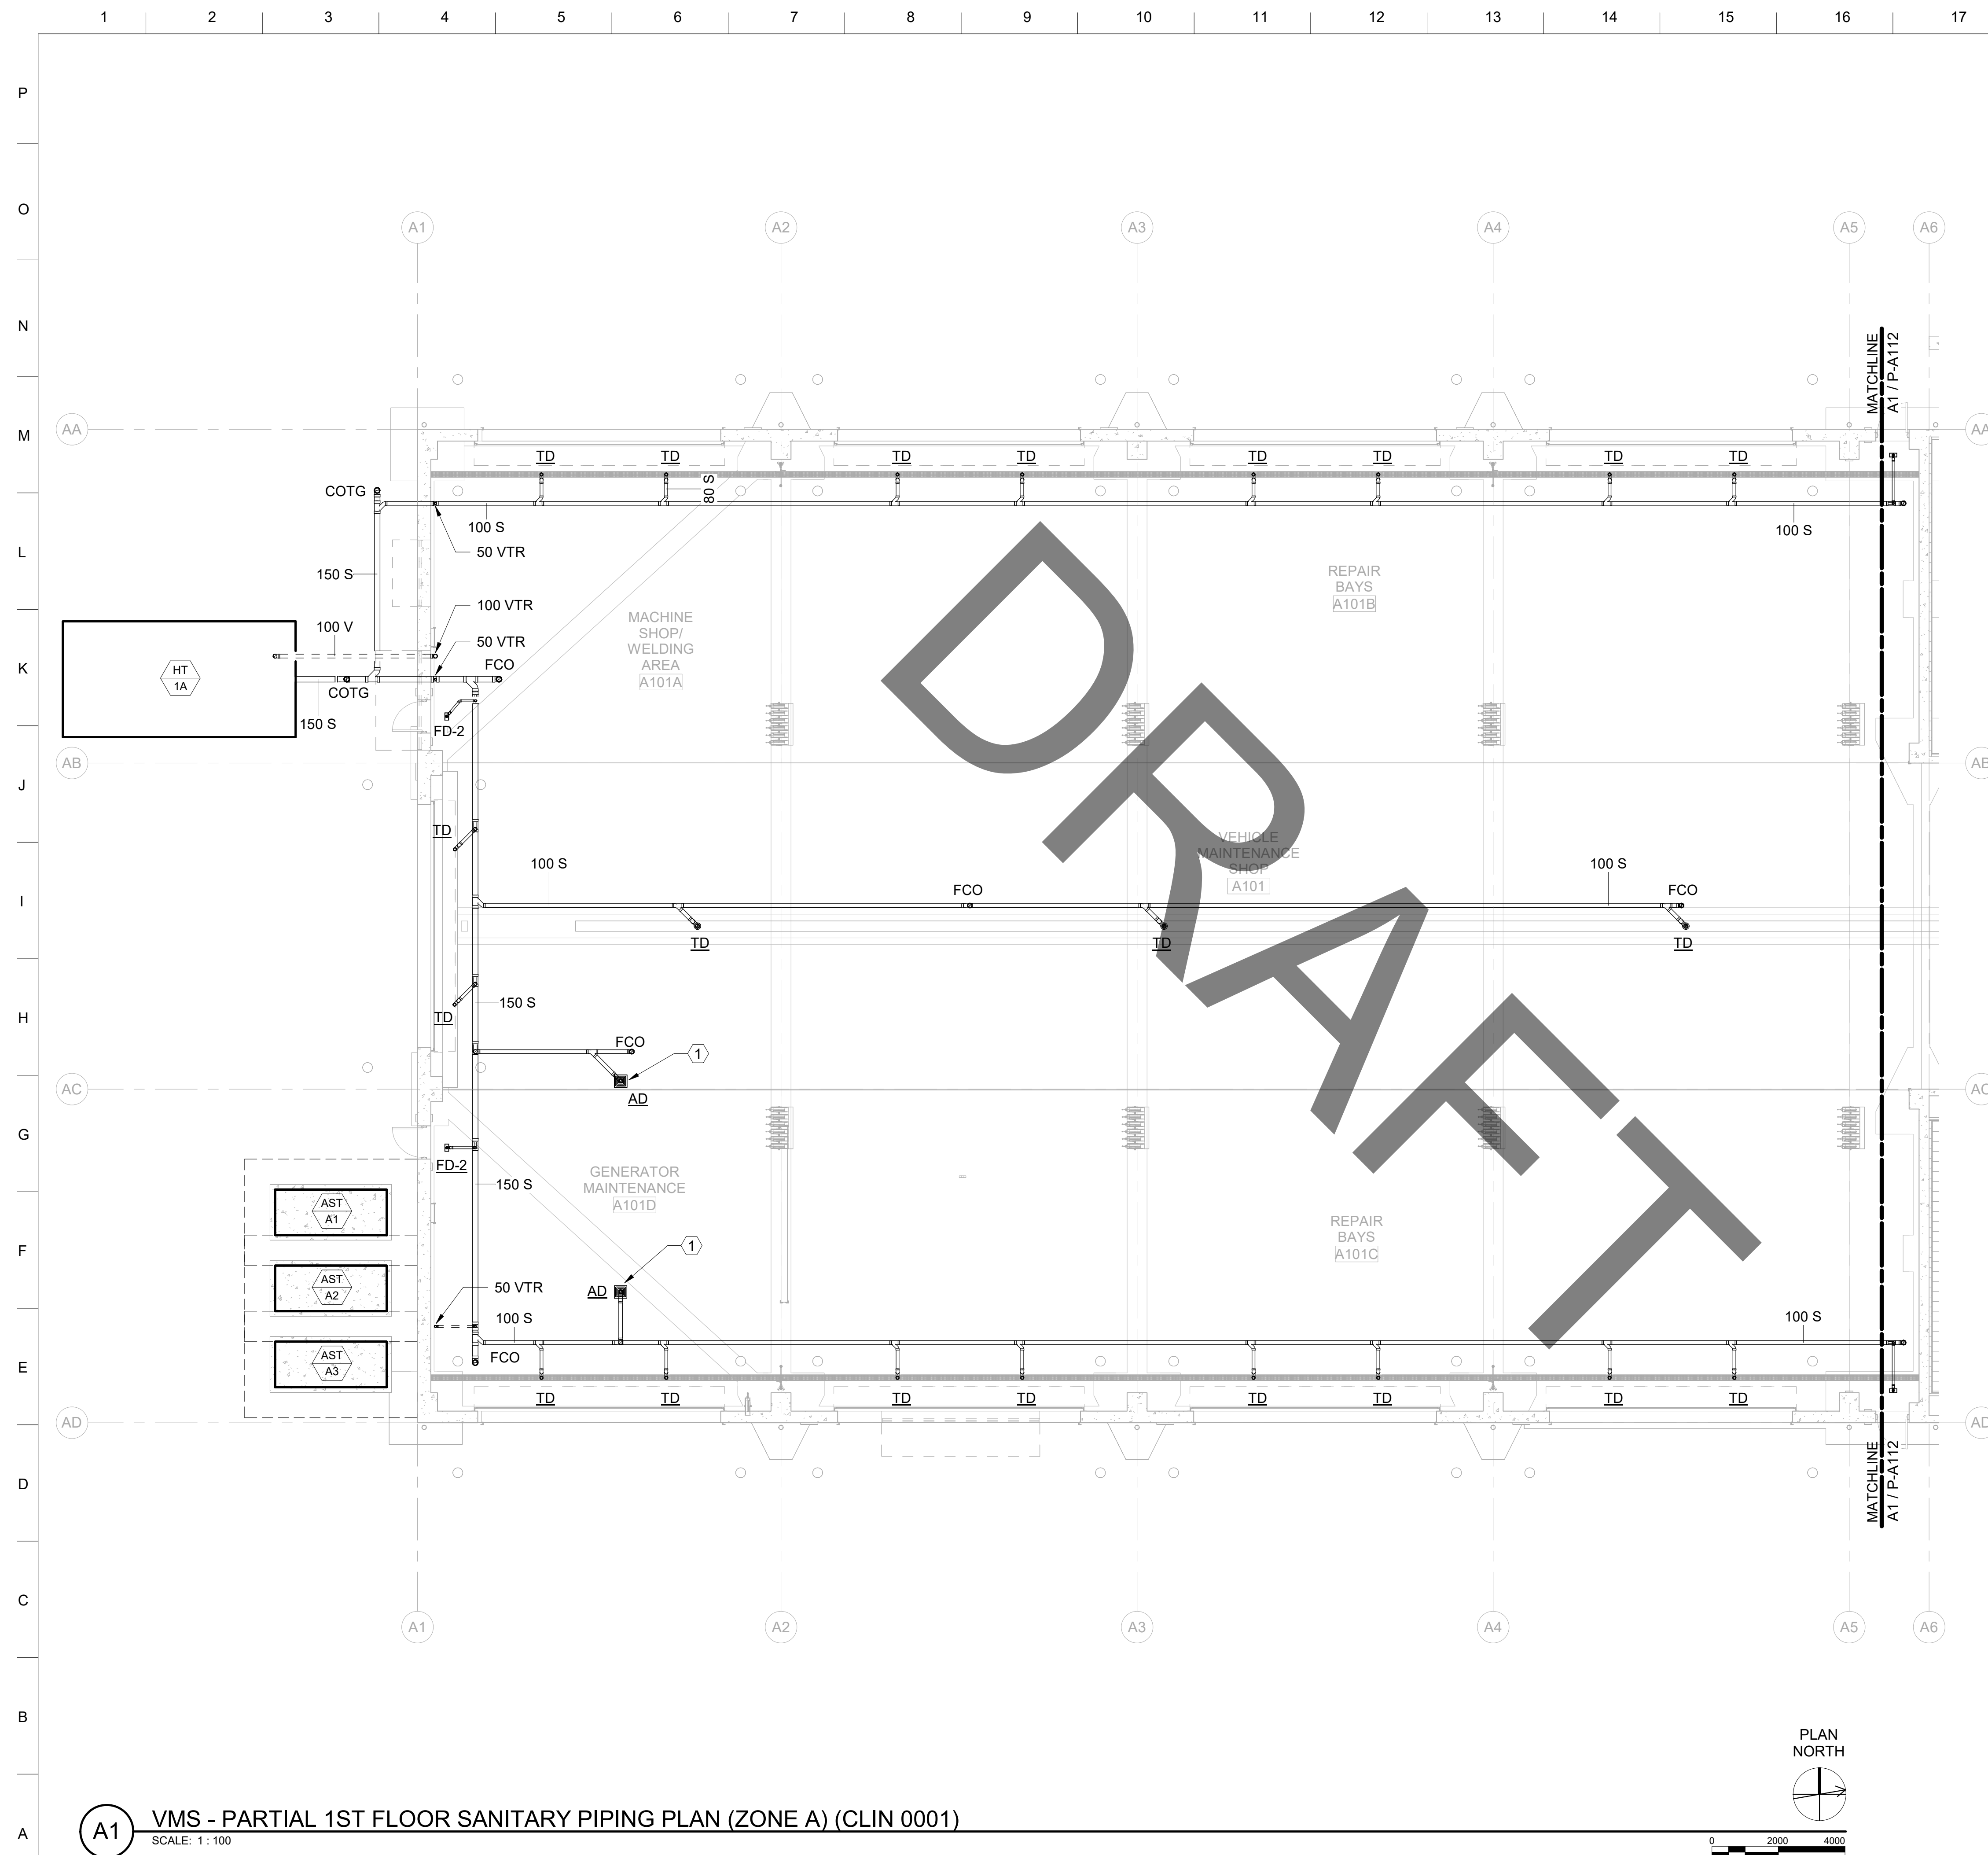

KEY NOTES

1 LARGE CAPACITY DRAIN BOX, TYPICAL.



US Army Corps
of Engineers ®

[illegible]

DESIGNED BY: US ARMY CORPS OF ENGINEERS JAPAN ENGINEER DISTRICT OKINAWA AREA OFFICE APO AP 96376-5132	DESIGNED BY:	ISSUE DATE:
	DRAWN BY:	
	CHECKED BY:	
	CONTRACT NO.:	
DESIGN PARTNERS INCORPORATED 1580 MAKALOA STREET, SUITE 1100 HONOLULU, HAWAII 96814	BY: R. BALIGNASAY	SOLICITATION NO.:
	BY: O. CRABTREE	CONTRACT NO.:
	CHECKED BY:	W912HV-17-D-0003
	SIZE:	
	ANSI D	

FY20 MCA PN77833 VEHICLE MAINTENANCE SHOP
KADENA AIR BASE, OKINAWA, JAPAN


SHEET ID


P-A111

INTERMEDIATE DESIGN

C:\Users\rbalignasay\Documents\511758_TEMF_PLUMB_v2022_rbalignasay.rvt

Plot Date: 12/15/2025 1:18:26 PM File Path:

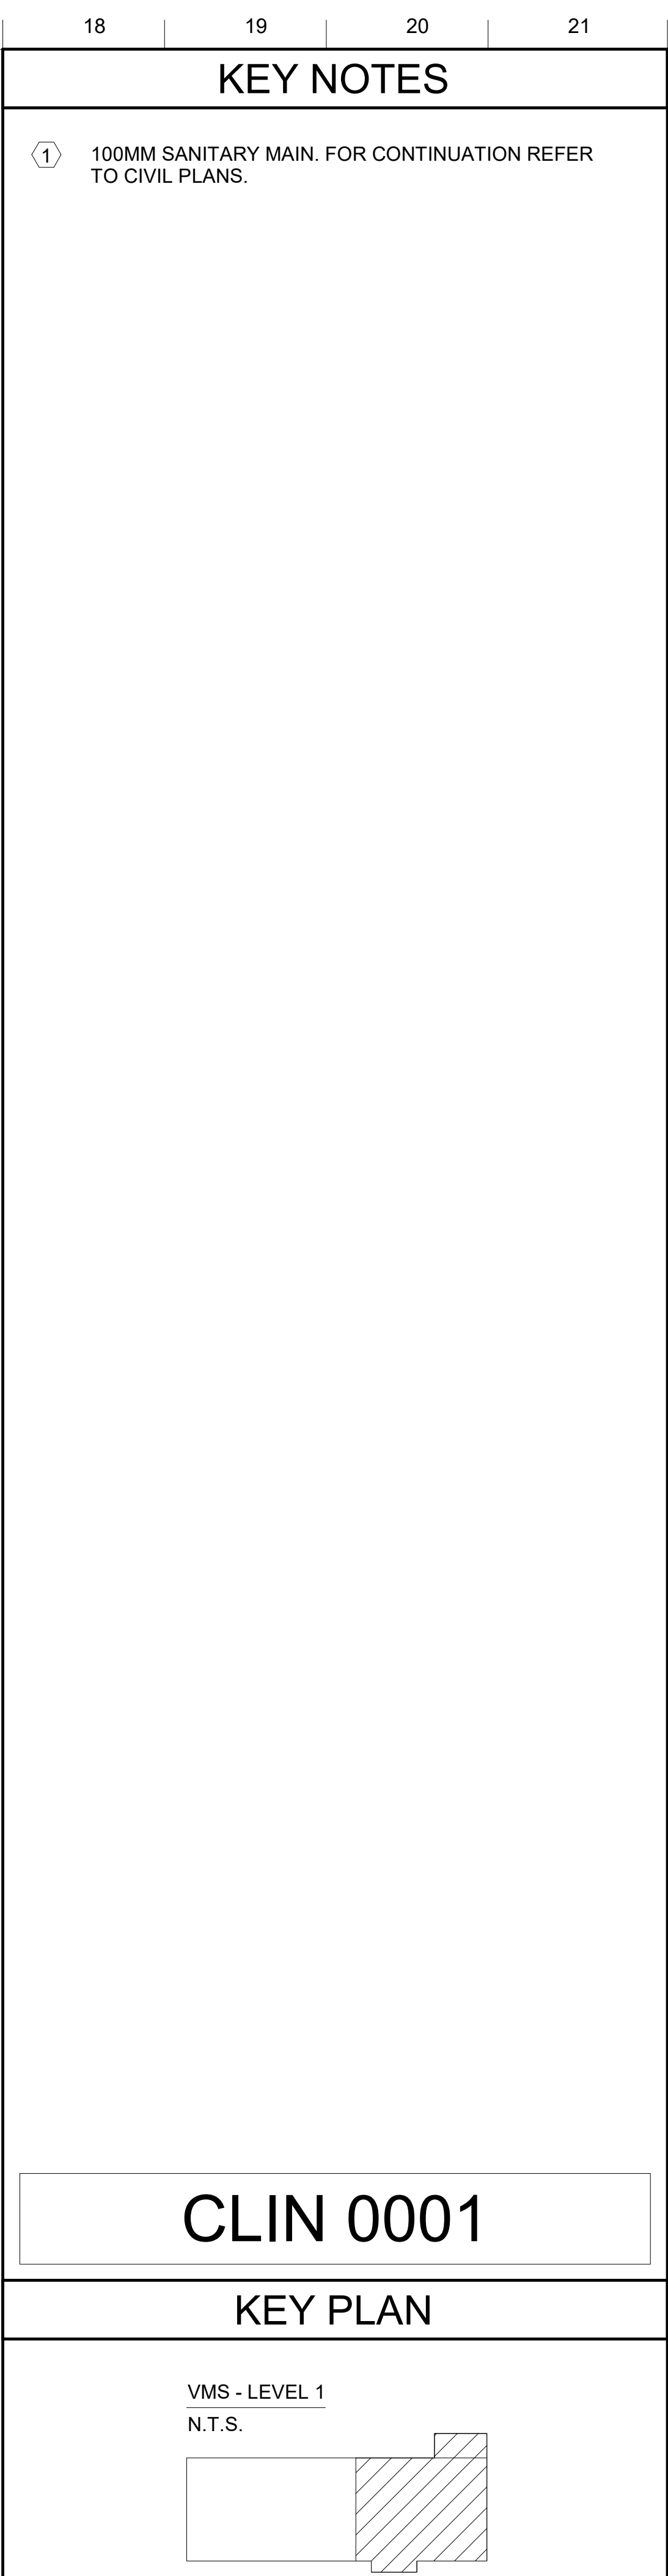

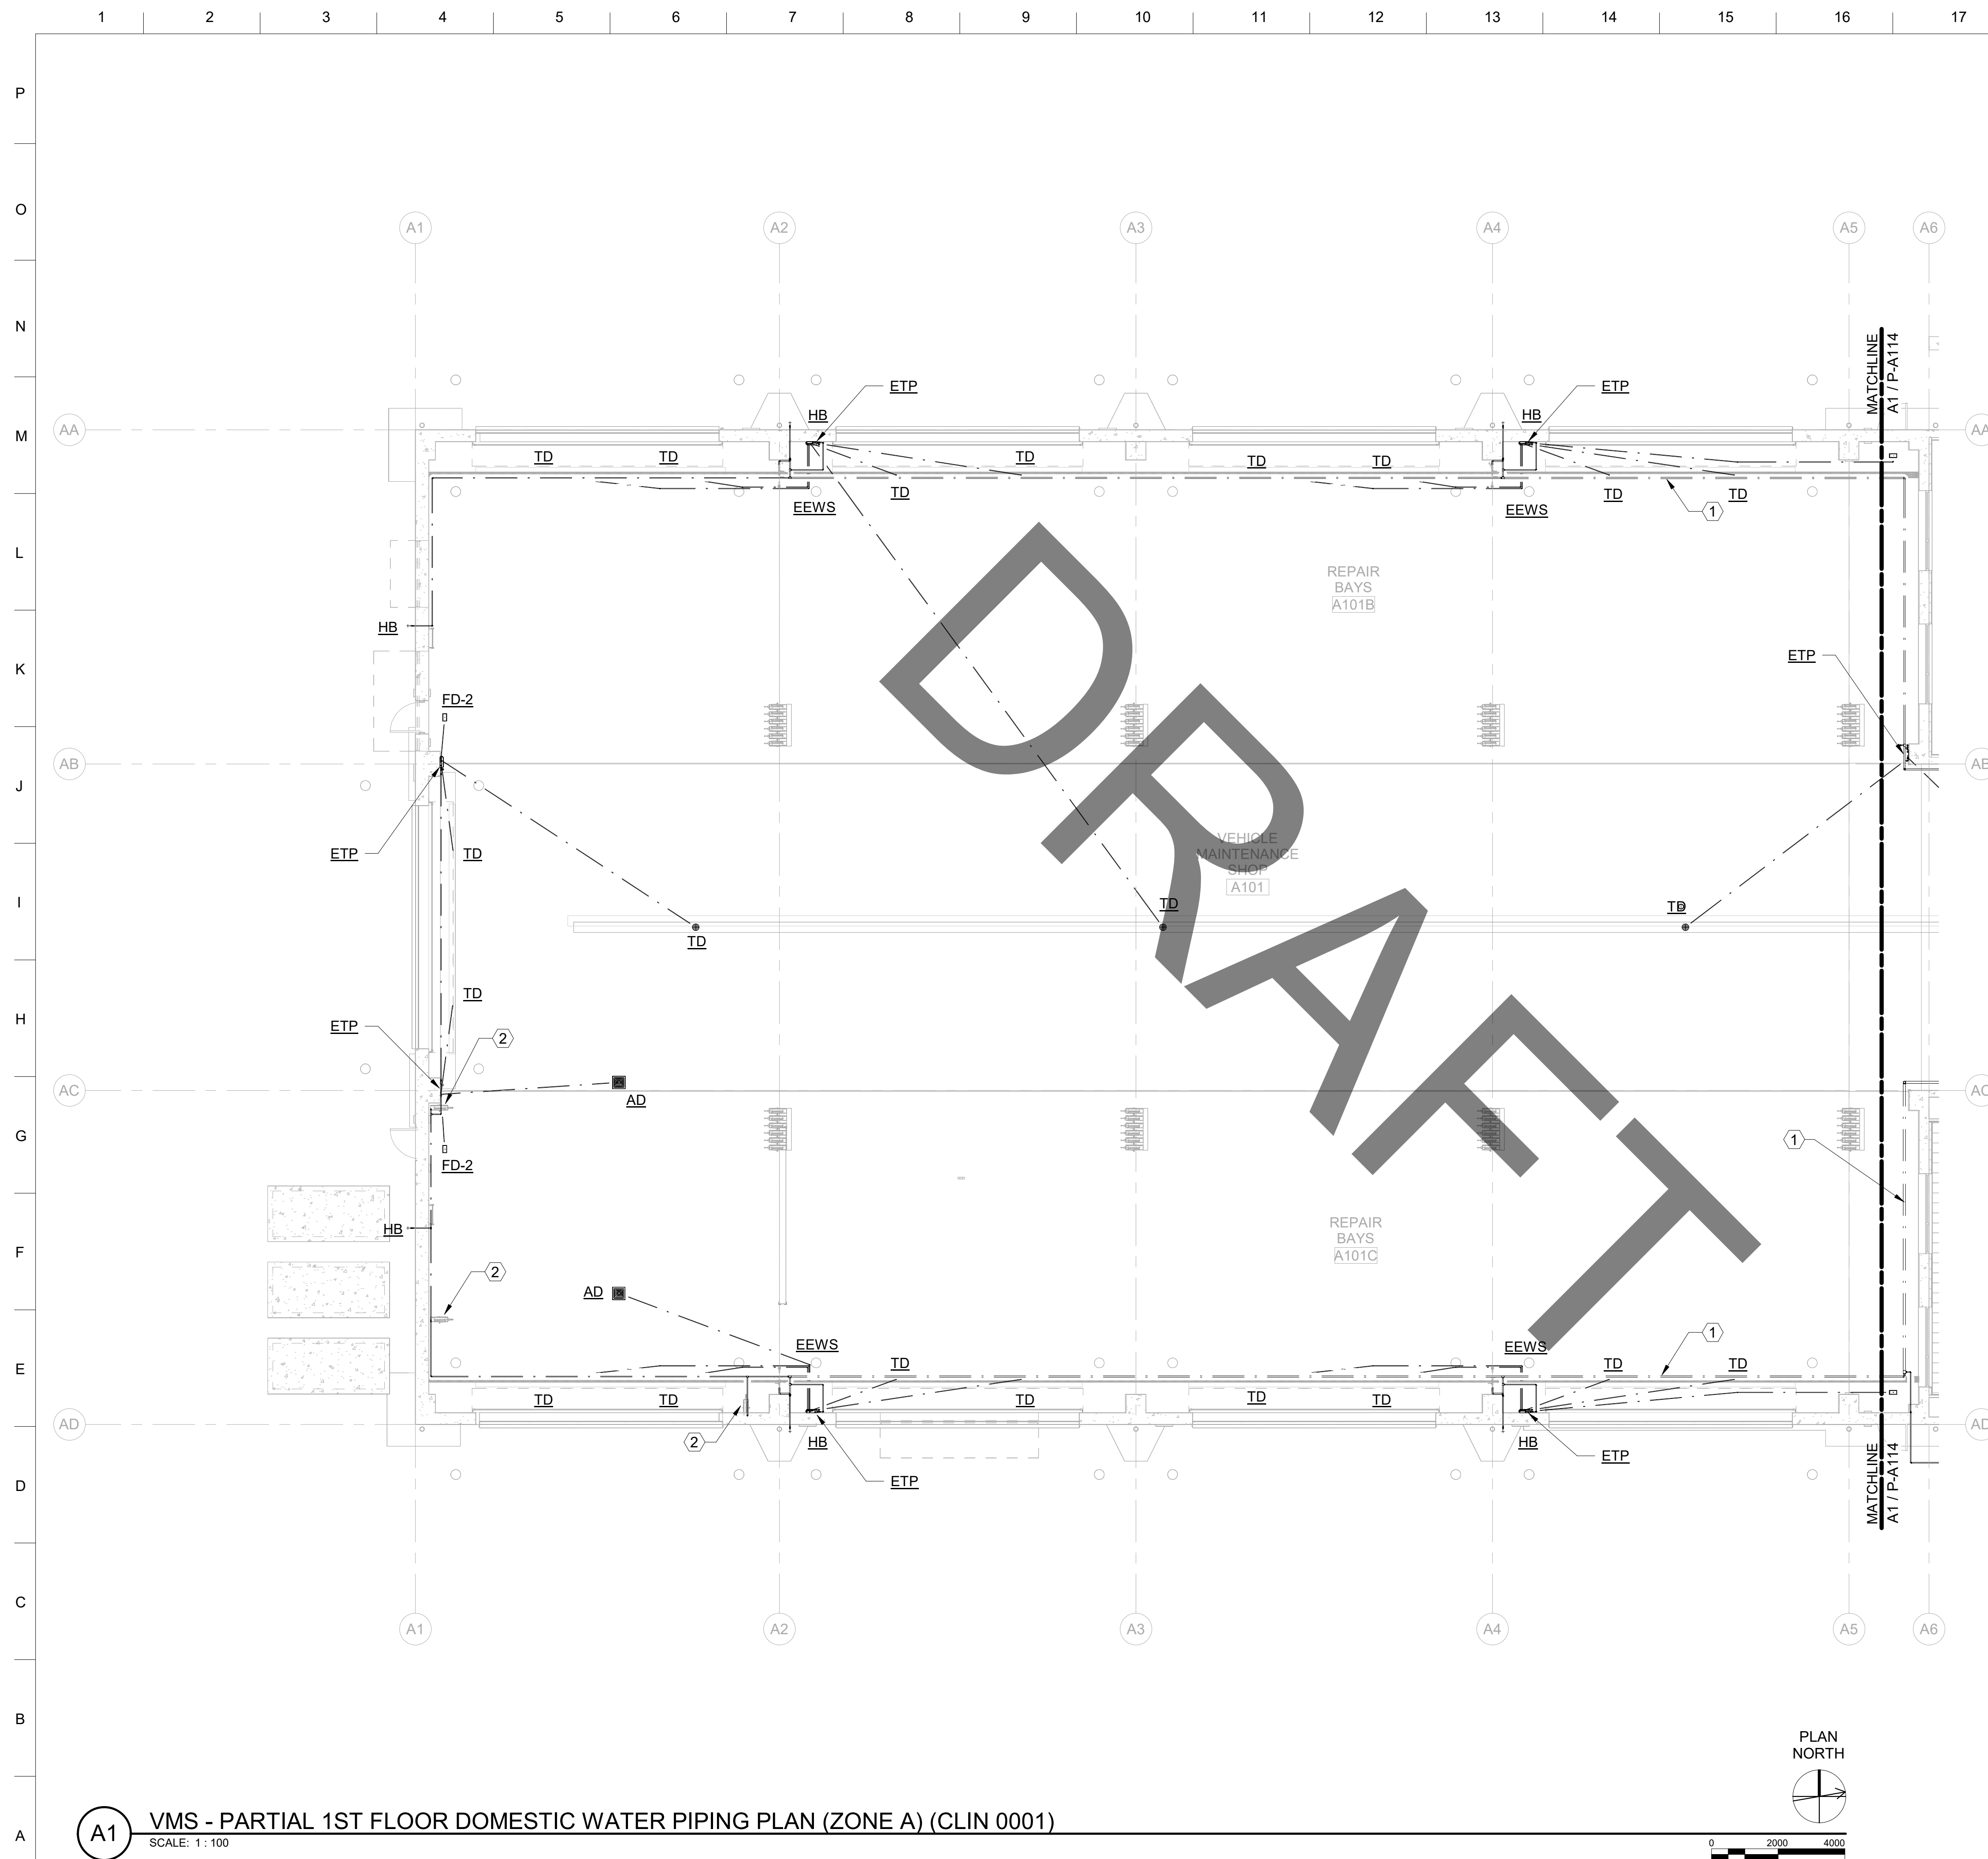

KEY NOTES

- ① ROUTE CW PIPING HIGH TO CLEAR WORK BAY ROLL UP DOORS, TYPICAL.
- ② WASH DOWN HOSE REEL, TYPICAL OF 3.



**US Army Corps
of Engineers®**

[illegible]

US ARMY CORPS OF ENGINEERS JAPAN ENGINEER DISTRICT OKINAWA AREA OFFICE APO AP 96376-5132	DESIGNED BY: I. TSANG	ISSUE DATE:
DESIGN PARTNERS, INCORPORATED 1500 HAKALO STREET, SUITE 1100 HONOLULU, HAWAII 96814	DRAWN BY: R. BALIGNASAY	SOLICITATION NO.:
	CHECKED BY: O. CRABTREE	CONTRACT NO.:
	SUBMITTED BY:	W912HV-17-D-0003
	SIZE:	

Plot Date: 12/15/2025 1:18:37 PM File Path:

C:\Users\rbfaligassay\Documents\511758 TEMF PLUMB v2022_rbfaligassay.m

INTERMEDIATE DESIGN


FY20 MCA PN77833 VEHICLE MAINTENANCE SHOP
 KADENA AIR BASE, OKINAWA, JAPAN

SHEET ID
P-A113


CLIN 0001


KEY PLAN

VMS - LEVEL 1
N.T.S.

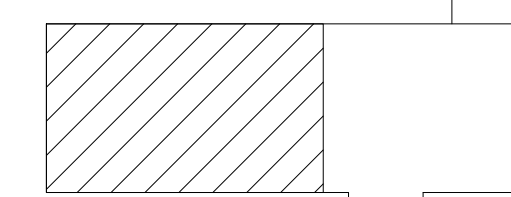

PLAN
NORTH

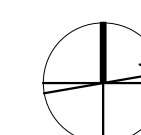

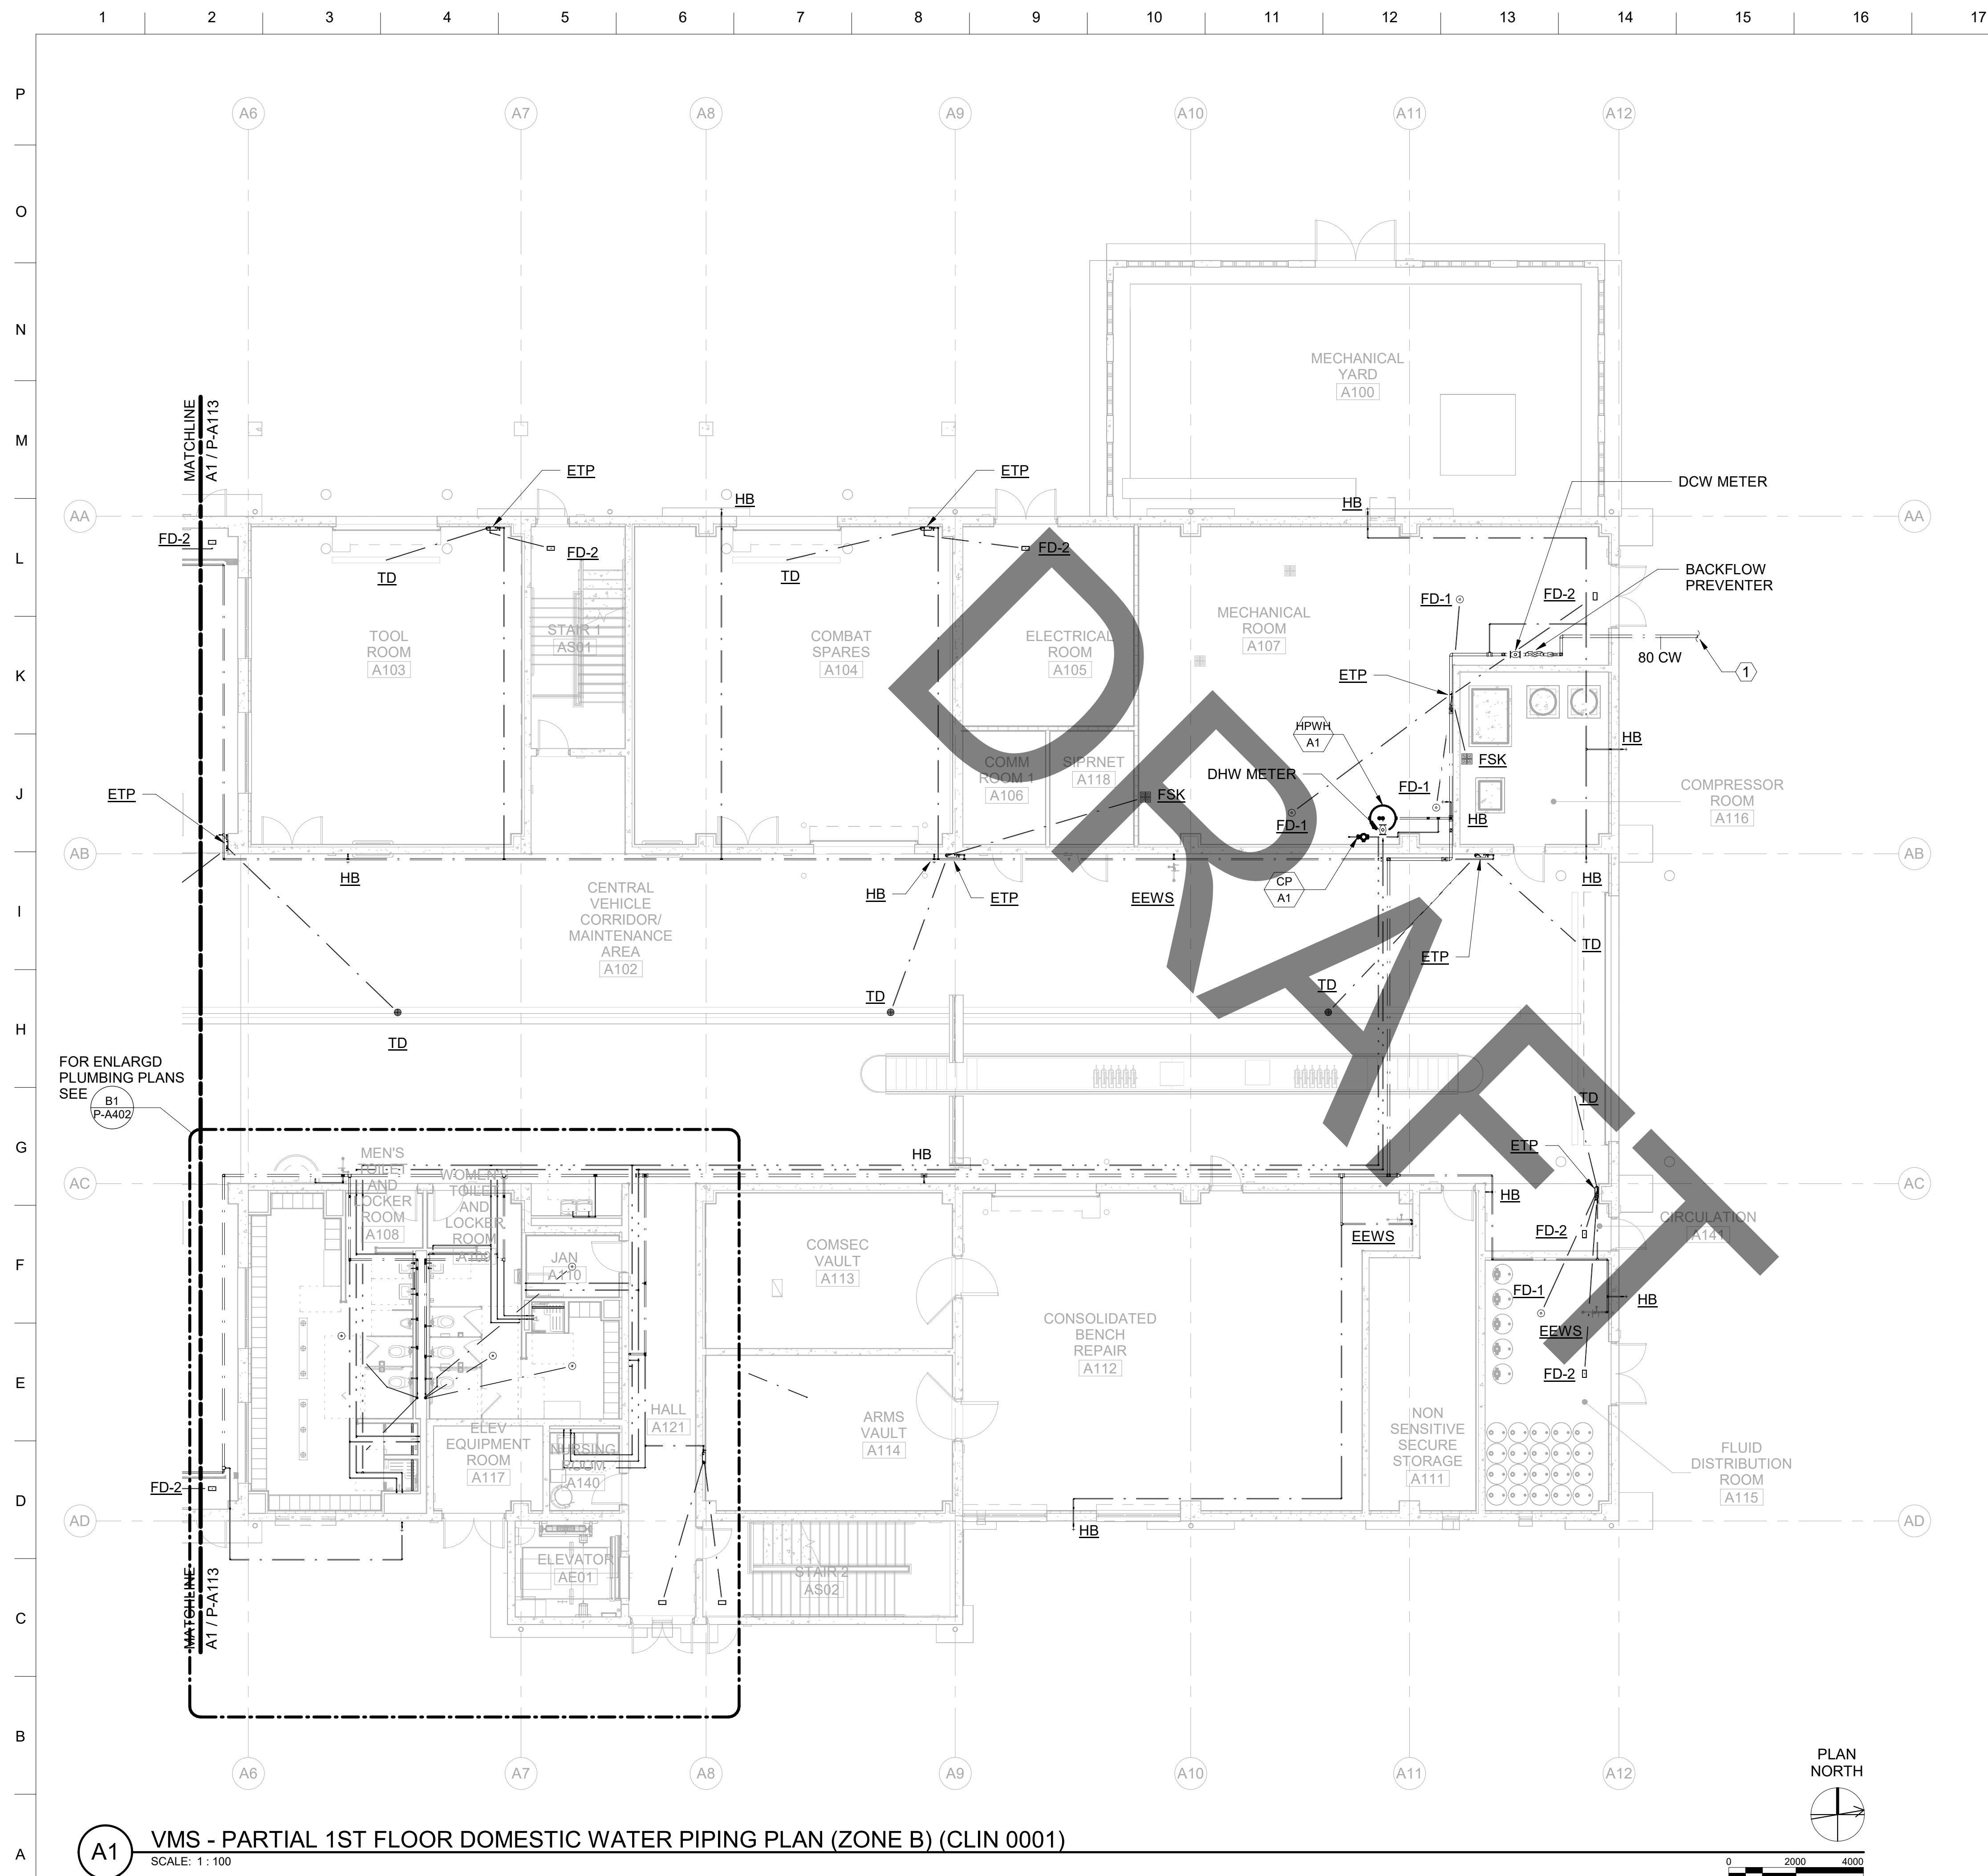

KEY NOTES

1 80MM DOMESTIC CW MAIN. REFER TO CIVIL FOR CONTINUATION.

US Army Corps
of Engineers ®[illegible]

US ARMY CORPS OF ENGINEERS JAPAN ENGINEER DISTRICT OKINAWA AREA OFFICE APO AF 96376-5132	DESIGNED BY: DRAWN BY: R. BALIGANASY CHECKED BY: O. KRATZKE SUBMITTED BY: SIZE:	ISSUE DATE: SOLICITATION NO.: CONTRACT NO.: W9124W-17-D-0003
DESIGN PARTNERS INCORPORATED 1580 MAKALOA STREET, SUITE 1100 HONOLULU, HAWAII 96814		

VEY20 MCA PN77833 VEHICLE MAINTENANCE SHOP
KADENA AIR BASE, OKINAWA, JAPAN

VMS - PARTIAL 1ST FLOOR DOMESTIC WATER
PIPING PLAN (ZONE B) (CLIN 0001)

SHEET ID

P-A114

INTERMEDIATE DESIGN

Plot Date: 12/15/2025 1:18:43 PM File Path:

\\Users\rbfignasay\Documents\511758_TEMF_PLUMB_v2022_rbfignasay.m



- ① PROVIDE COMPRESSED AIR, ANTI-FREEZE, GEAR OIL, ENGINE OIL, TRANSMISSION FLUID, AND GREASE PIPING HIGH IN CEILING SPACE.
- ② FLOOR MOUNTED PREFABRICATED POL DISPENSING SINGLE/DUAL SERVICE COLUMN. PROVIDE RETRACTABLE HOSE REELS FOR COMPRESSED AIR, ANTI-FREEZE, GEAR OIL, ENGINE OIL, TRANSMISSION FLUID, AND GREASE. SERVICE COLUMN TO ALSO HAVE RETRACTABLE HOSE REELS FOR DOMESTIC COLD WATER AND HARD WIRE 120V EXTENSION CHORD.
- ③ ROUTE PIPING HIGH TO CLEAR WORK BAY ROLL UP DOORS, TYPICAL.
- ④ ROUTE PIPING IN TRENCH, (TYPICAL).

[illegible]

US ARMY CORPS OF ENGINEERS JANUARY 1971 OKAWA AREA OFFICE APO AF 96376-0132	DESIGNED BY: I T SANG	ISSUE DATE:
DESIGN PARTNERS, INCORPORATED 1560 MAKALOA STREET, SUITE 1100 HONOLULU, HAWAII 96814	DRAWN BY: MICHAEL KASSAY	SOLICITATION NO.:
	CHECKED BY: O C RABTREE	CONTRACT NO.: W912HV-17-D-0003
	SUBMITTED BY:	
	SIZE: ANSI D	

FY20 MCA PN77833 VEHICLE MAINTENANCE SHOP
KADENA AIR BASE, OKINAWA, JAPAN


SHEET ID

P-A115

CLIN 0001

KEY PLAN


VMS - LEVEL 1
N.T.S.

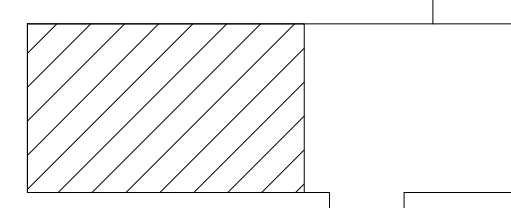

INTERMEDIATE DESIGN

Plot Date: 12/15/2025 1:18:48 PM

C:\Users\rba\ignasay\Documents\511758_TEMF_PLUMB_v2022_rba\ignasay.rvt

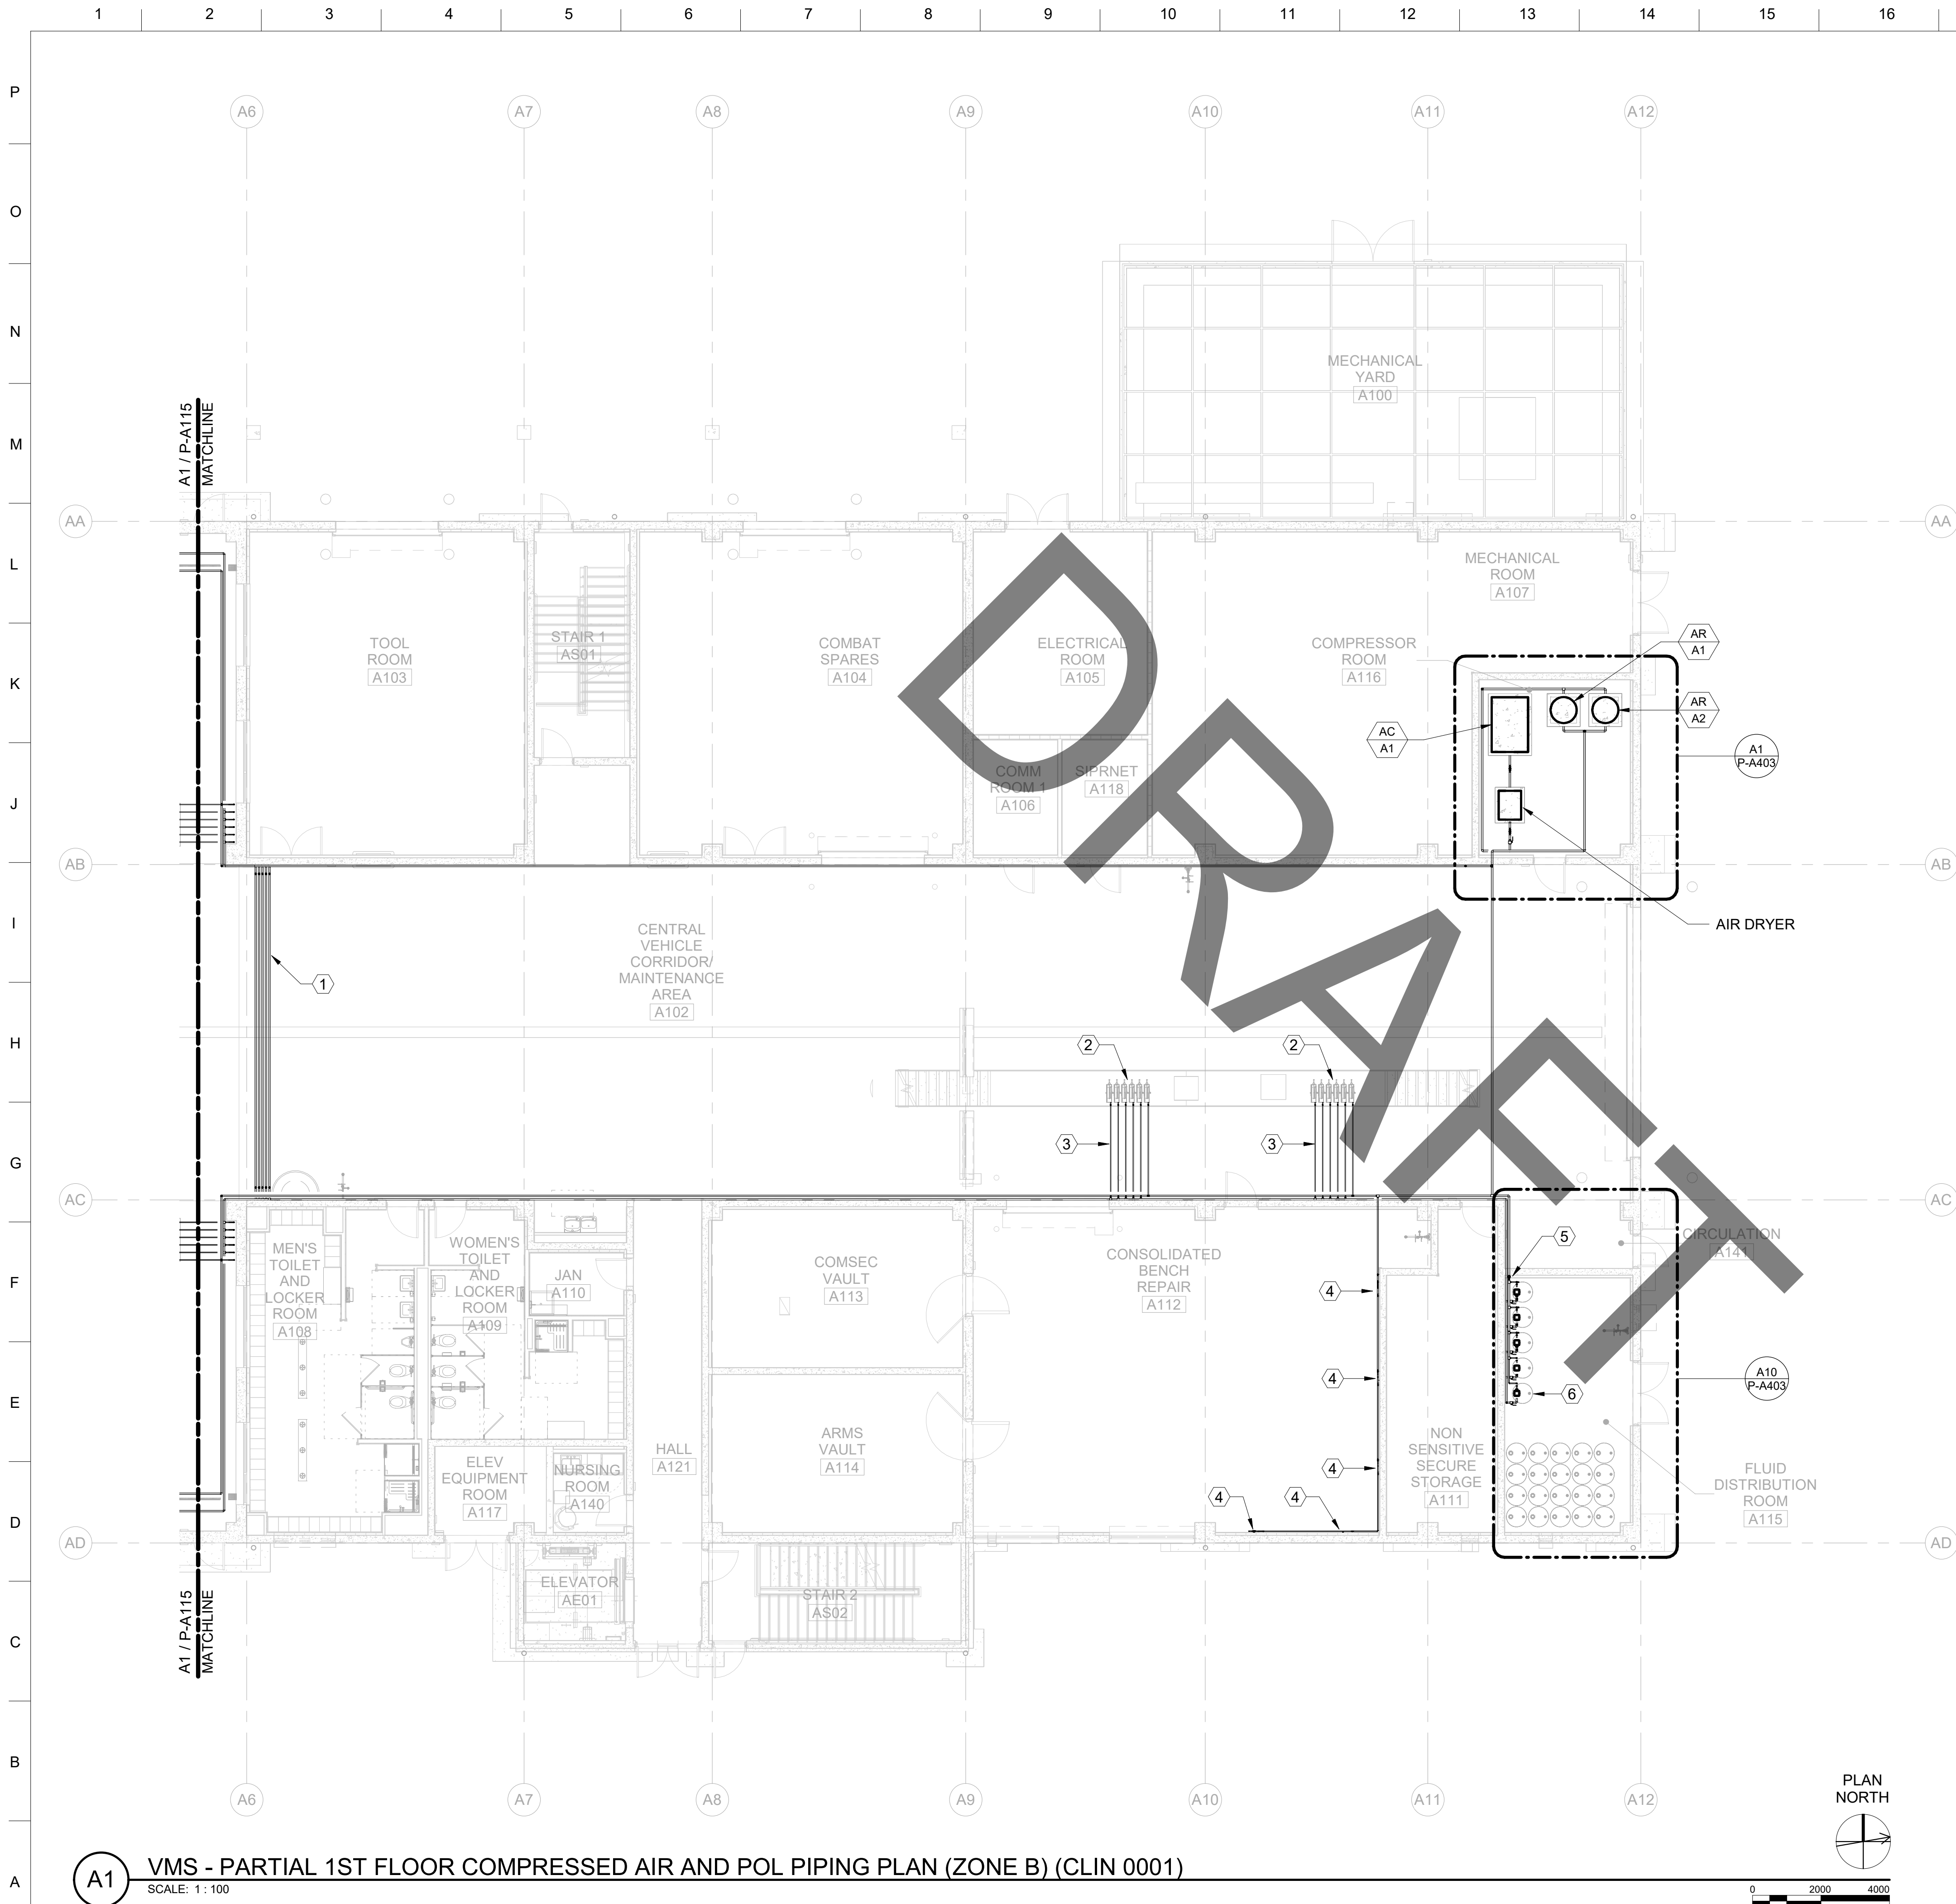

A1 VMS - PARTIAL 1ST FLOOR COMPRESSED AIR AND POL PIPING PLAN (ZONE B) (CLIN 0001)
SCALE: 1 : 100

KEY NOTES

- 1 PROVIDE COMPRESSED AIR, ANTI-FREEZE, GEAR OIL, ENGINE OIL, TRANSMISSION FLUID, AND GREASE PIPING HIGH IN CEILING SPACE.
- 2 FLOOR MOUNTED PREFABRICATED POL DISPENSING SINGLE/DUAL SERVICE COLUMN. PROVIDE RETRACTIBLE HOSE REELS FOR COMPRESSED AIR, ANTI-FREEZE, GEAR OIL, ENGINE OIL, TRANSMISSION FLUID, AND GREASE. SERVICE COLUMN TO ALSO HAVE RETRACTIBLE HOSE REELS FOR DOMESTIC COLD WATER AND HARD WIRE 120V EXTENSION CHORD.
- 3 ROUTE PIPING IN TRENCH, (TYPICAL).
- 4 COMPRESS AIR STATION, TYPICAL OF 5.
- 5 COMPRESSED AIR DN TO POL PUMPS, TYPICAL.
- 6 ANTI-FREEZE, GEAR OIL, ENGINE OIL, TRANSMISSION FLUID, AND GREASE DRUMS, TYPICAL.



US Army Corps
of Engineers ®

DATE	DESCRIPTION	MARK

DESIGNED BY: I. TSANG	ISSUE DATE:
DRAWN BY: R. BALIGASAY	SOLICITATION NO.:
CHECKED BY: W. J. J. J.	CONTRACT NO.:
SUBMITTED BY:	W72WY-17-D-0003
SIZE: ANSI D	

US ARMY CORPS OF ENGINEERS
JAPAN ENGINEER DISTRICT
OKINAWA AREA OFFICE
APO AF 96376-5132

DESIGN PARTNERS INCORPORATED
1580 MAKALOA STREET, SUITE 1100
HONOLULU, HAWAII 96814


FY20 MCA PN7833 VEHICLE MAINTENANCE SHOP KADENA AIR BASE, OKINAWA, JAPAN	VMS - PARTIAL 1ST FLOOR COMPRESSED AIR AND POL PIPING PLAN (ZONE B) (CLIN 0001)
---	--

SHEET ID

P-A116

INTERMEDIATE DESIGN

Plot Date: 12/15/2025 1:18:54 PM File Path: C:\Users\baligasay\Documents\51178_PUMP_PLUMB_2022_baligasay.rvt

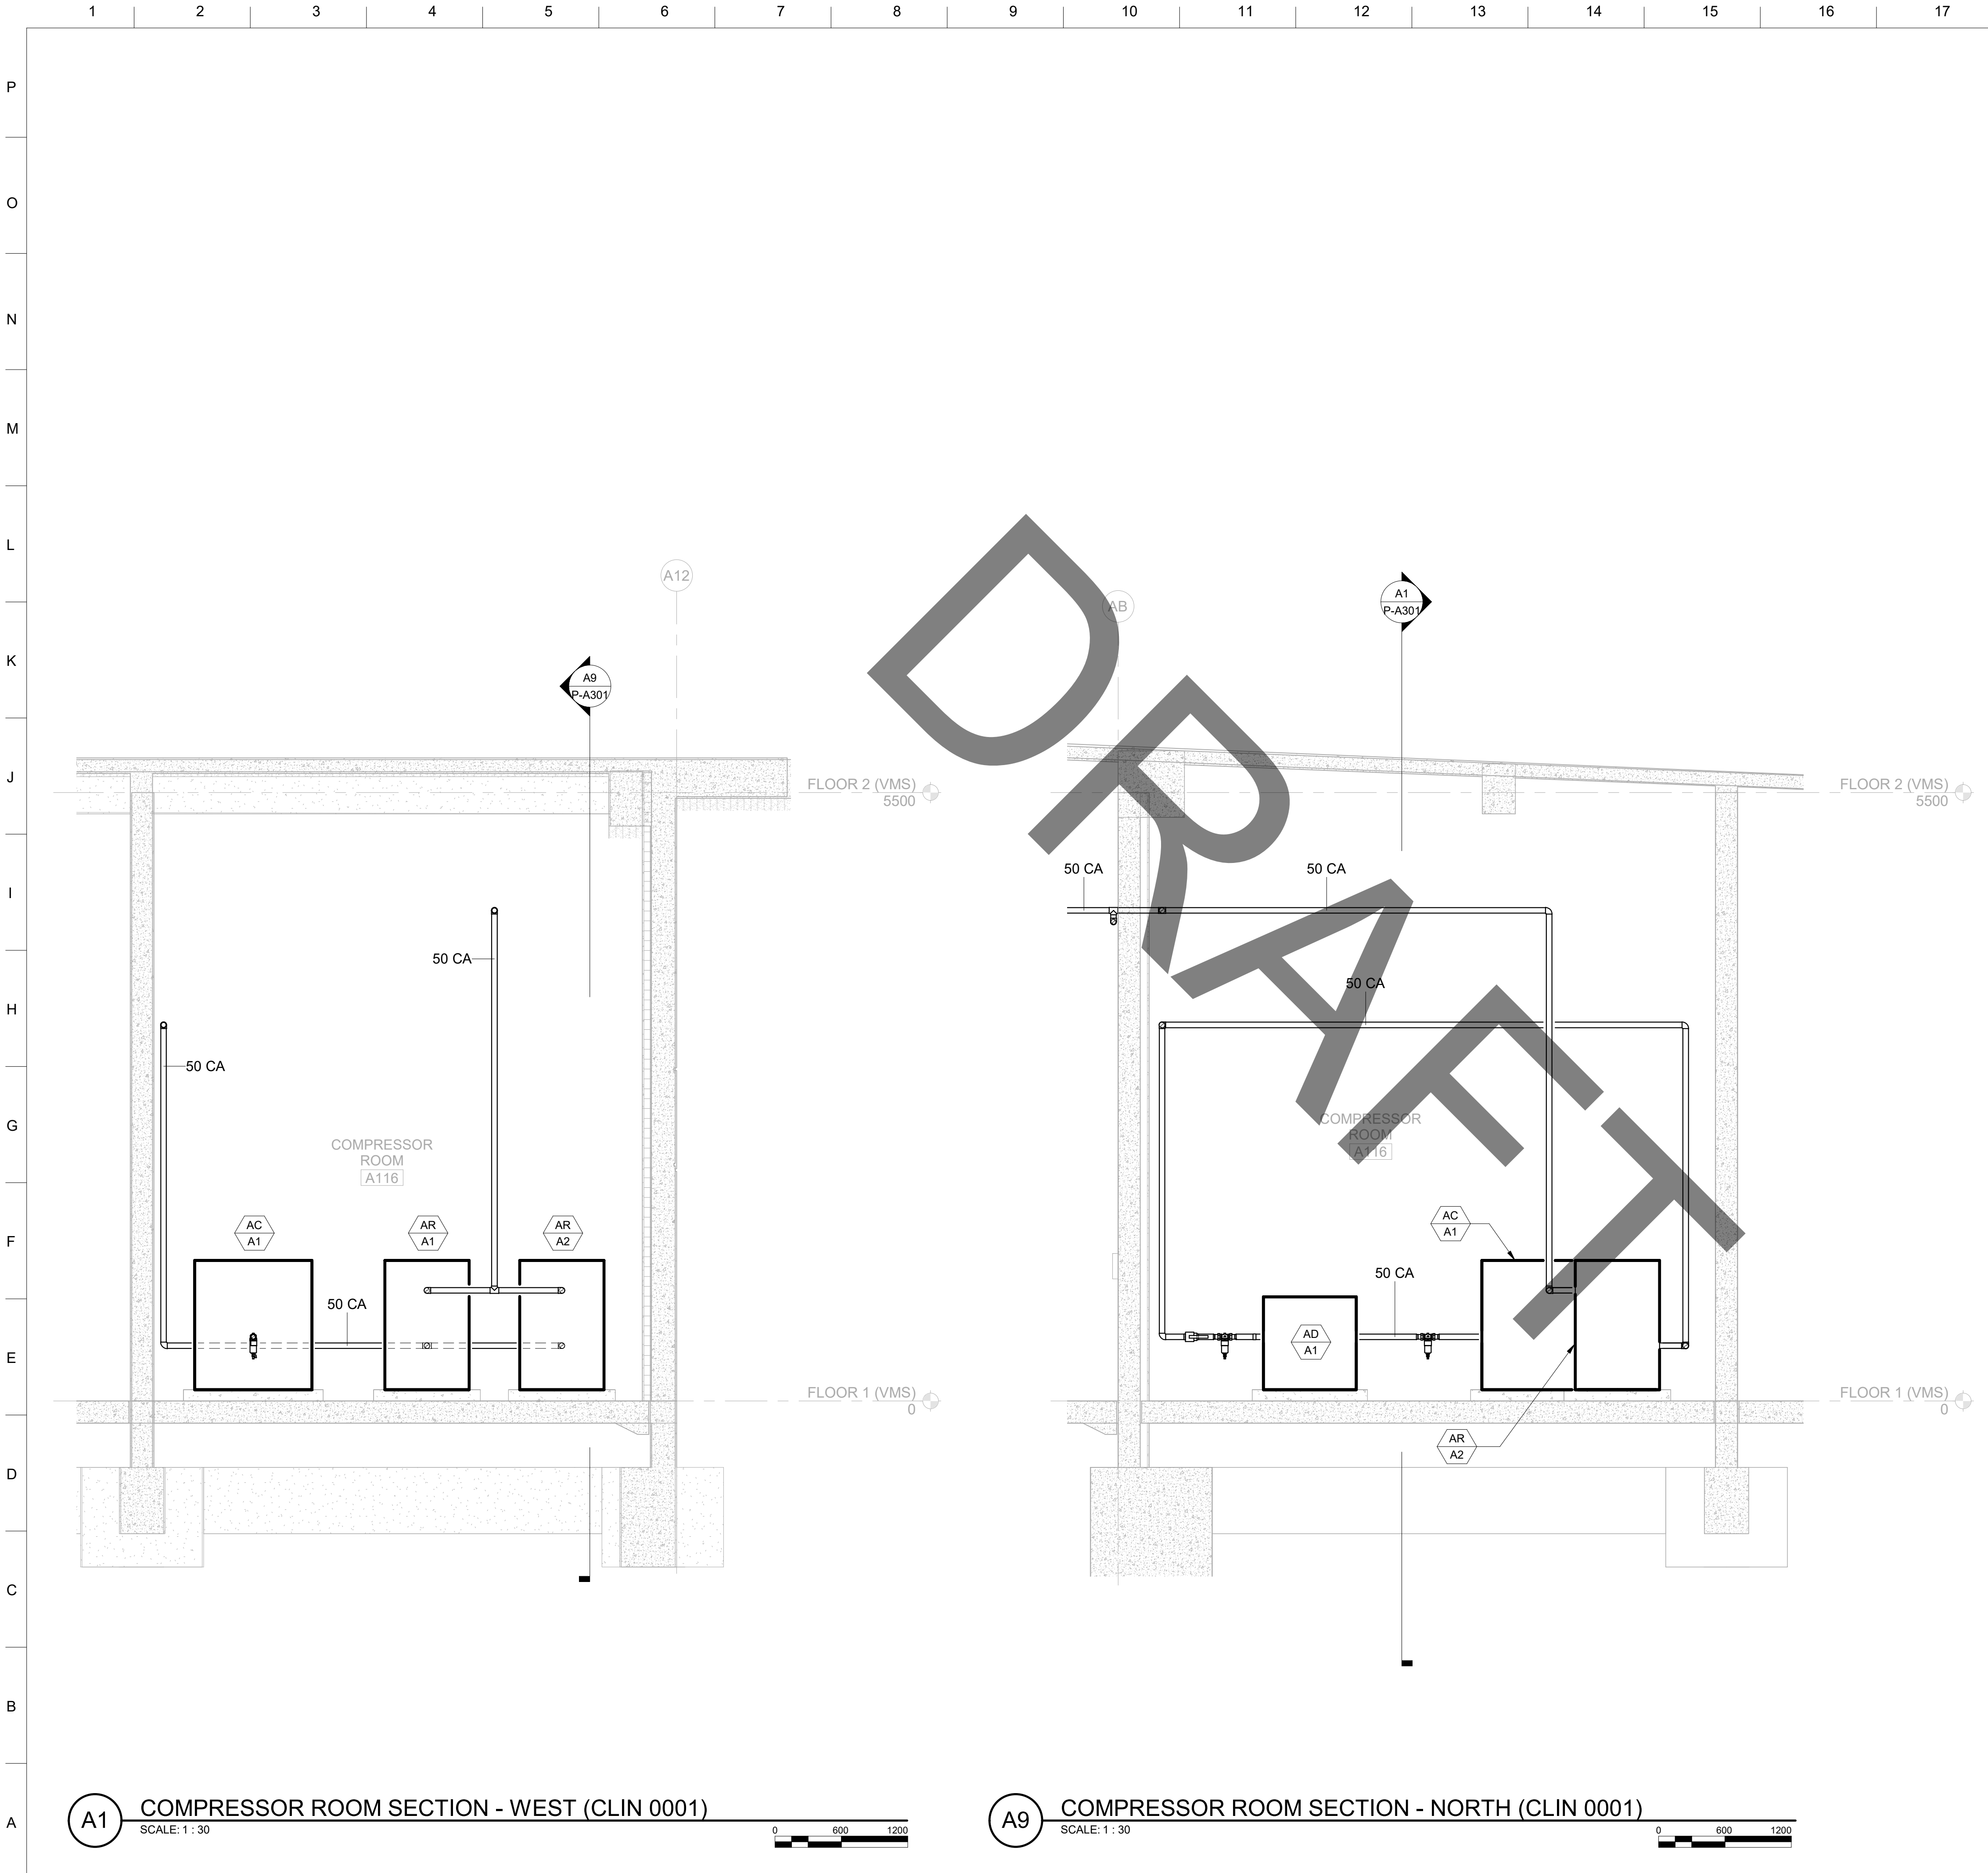

KEY NOTES

1 -



US Army Corps of Engineers ®

MARK	DESCRIPTION	DATE

DESIGNED BY: I. TSANG	ISSUE DATE:
DRAWN BY: R. BALIGASAY	SOLICITATION NO.:
CHECKED BY: R. BALIGASAY	CONTRACT NO.:
SUBMITTED BY:	W72WY-17-D-0003
SIZE: ANSI D	

US ARMY CORPS OF ENGINEERS JAPAN ENGINEER DISTRICT OKINAWA AREA OFFICE APO AF 96376-5132	
DESIGN PARTNERS INCORPORATED 1580 MAKALOA STREET, SUITE 1100 HONOLULU, HAWAII 96814	

FY20 MCA PN7833 VEHICLE MAINTENANCE SHOP
KADENA AIR BASE, OKINAWA, JAPAN

VMS - PLUMBING SECTIONS (CLIN 0001)

SHEET ID

P-A301

CLIN 0001

A1 COMPRESSOR ROOM SECTION - WEST (CLIN 0001)
SCALE: 1 : 30





A9 COMPRESSOR ROOM SECTION - NORTH (CLIN 0001)
SCALE: 1 : 30





P-A302 SHEET ID		FYZ0 MCA P477933 VEHICLE MAINTENANCE SHOP KADENA AIR BASE, OKINAWA, JAPAN		VMS - PLUMBING SECTIONS (CLIN 0001)	
US ARMY CORPS OF ENGINEERS JAPAN ENGINEER DISTRICT OKINAWA AREA OFFICE APO AP 96376-5132		DESIGNED BY: J. I. SANG CHECKED BY: R. BALIGNASAY SUBMITTED BY: O. CRAETHREE		SOLICITATION NO.: CONTRACT NO.: W912H-V-17-D-0003	
DESIGN PARTNERS INCORPORATED 1580 MAKALOA STREET, SUITE 1100 HONOLULU, HAWAII 96814		SIZE: ANSI/D		MARK:	
				DATE:	

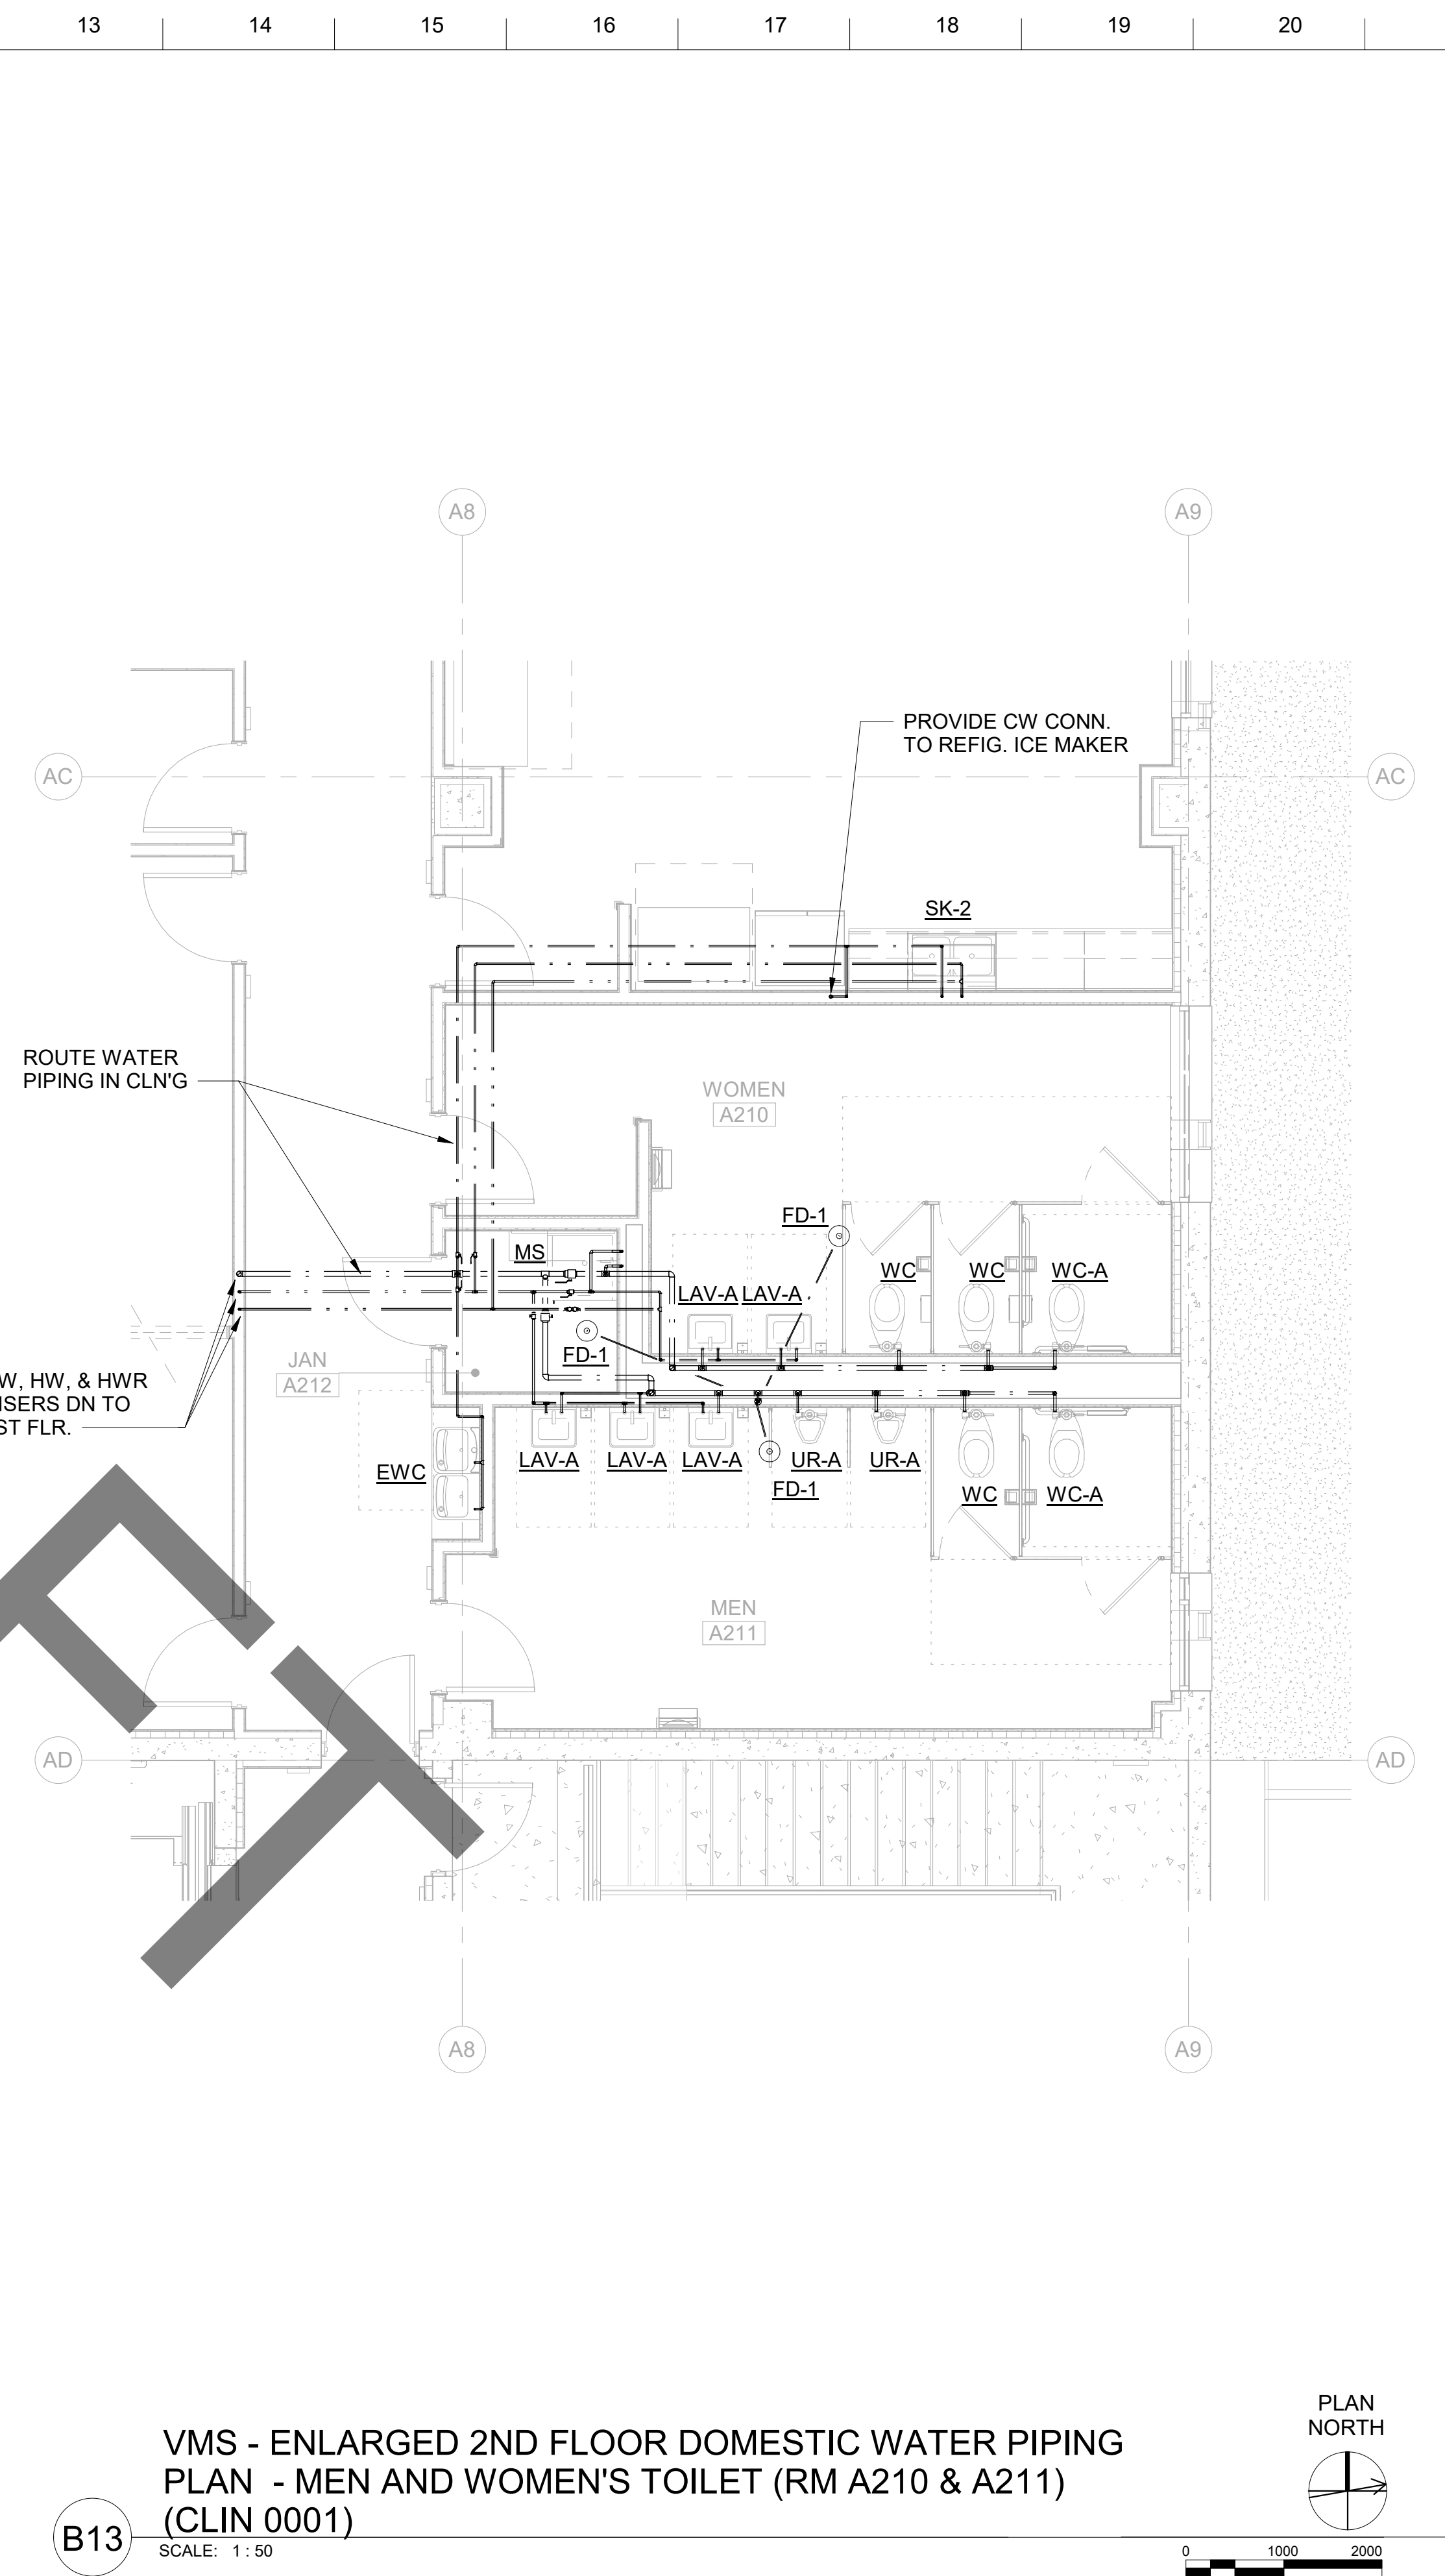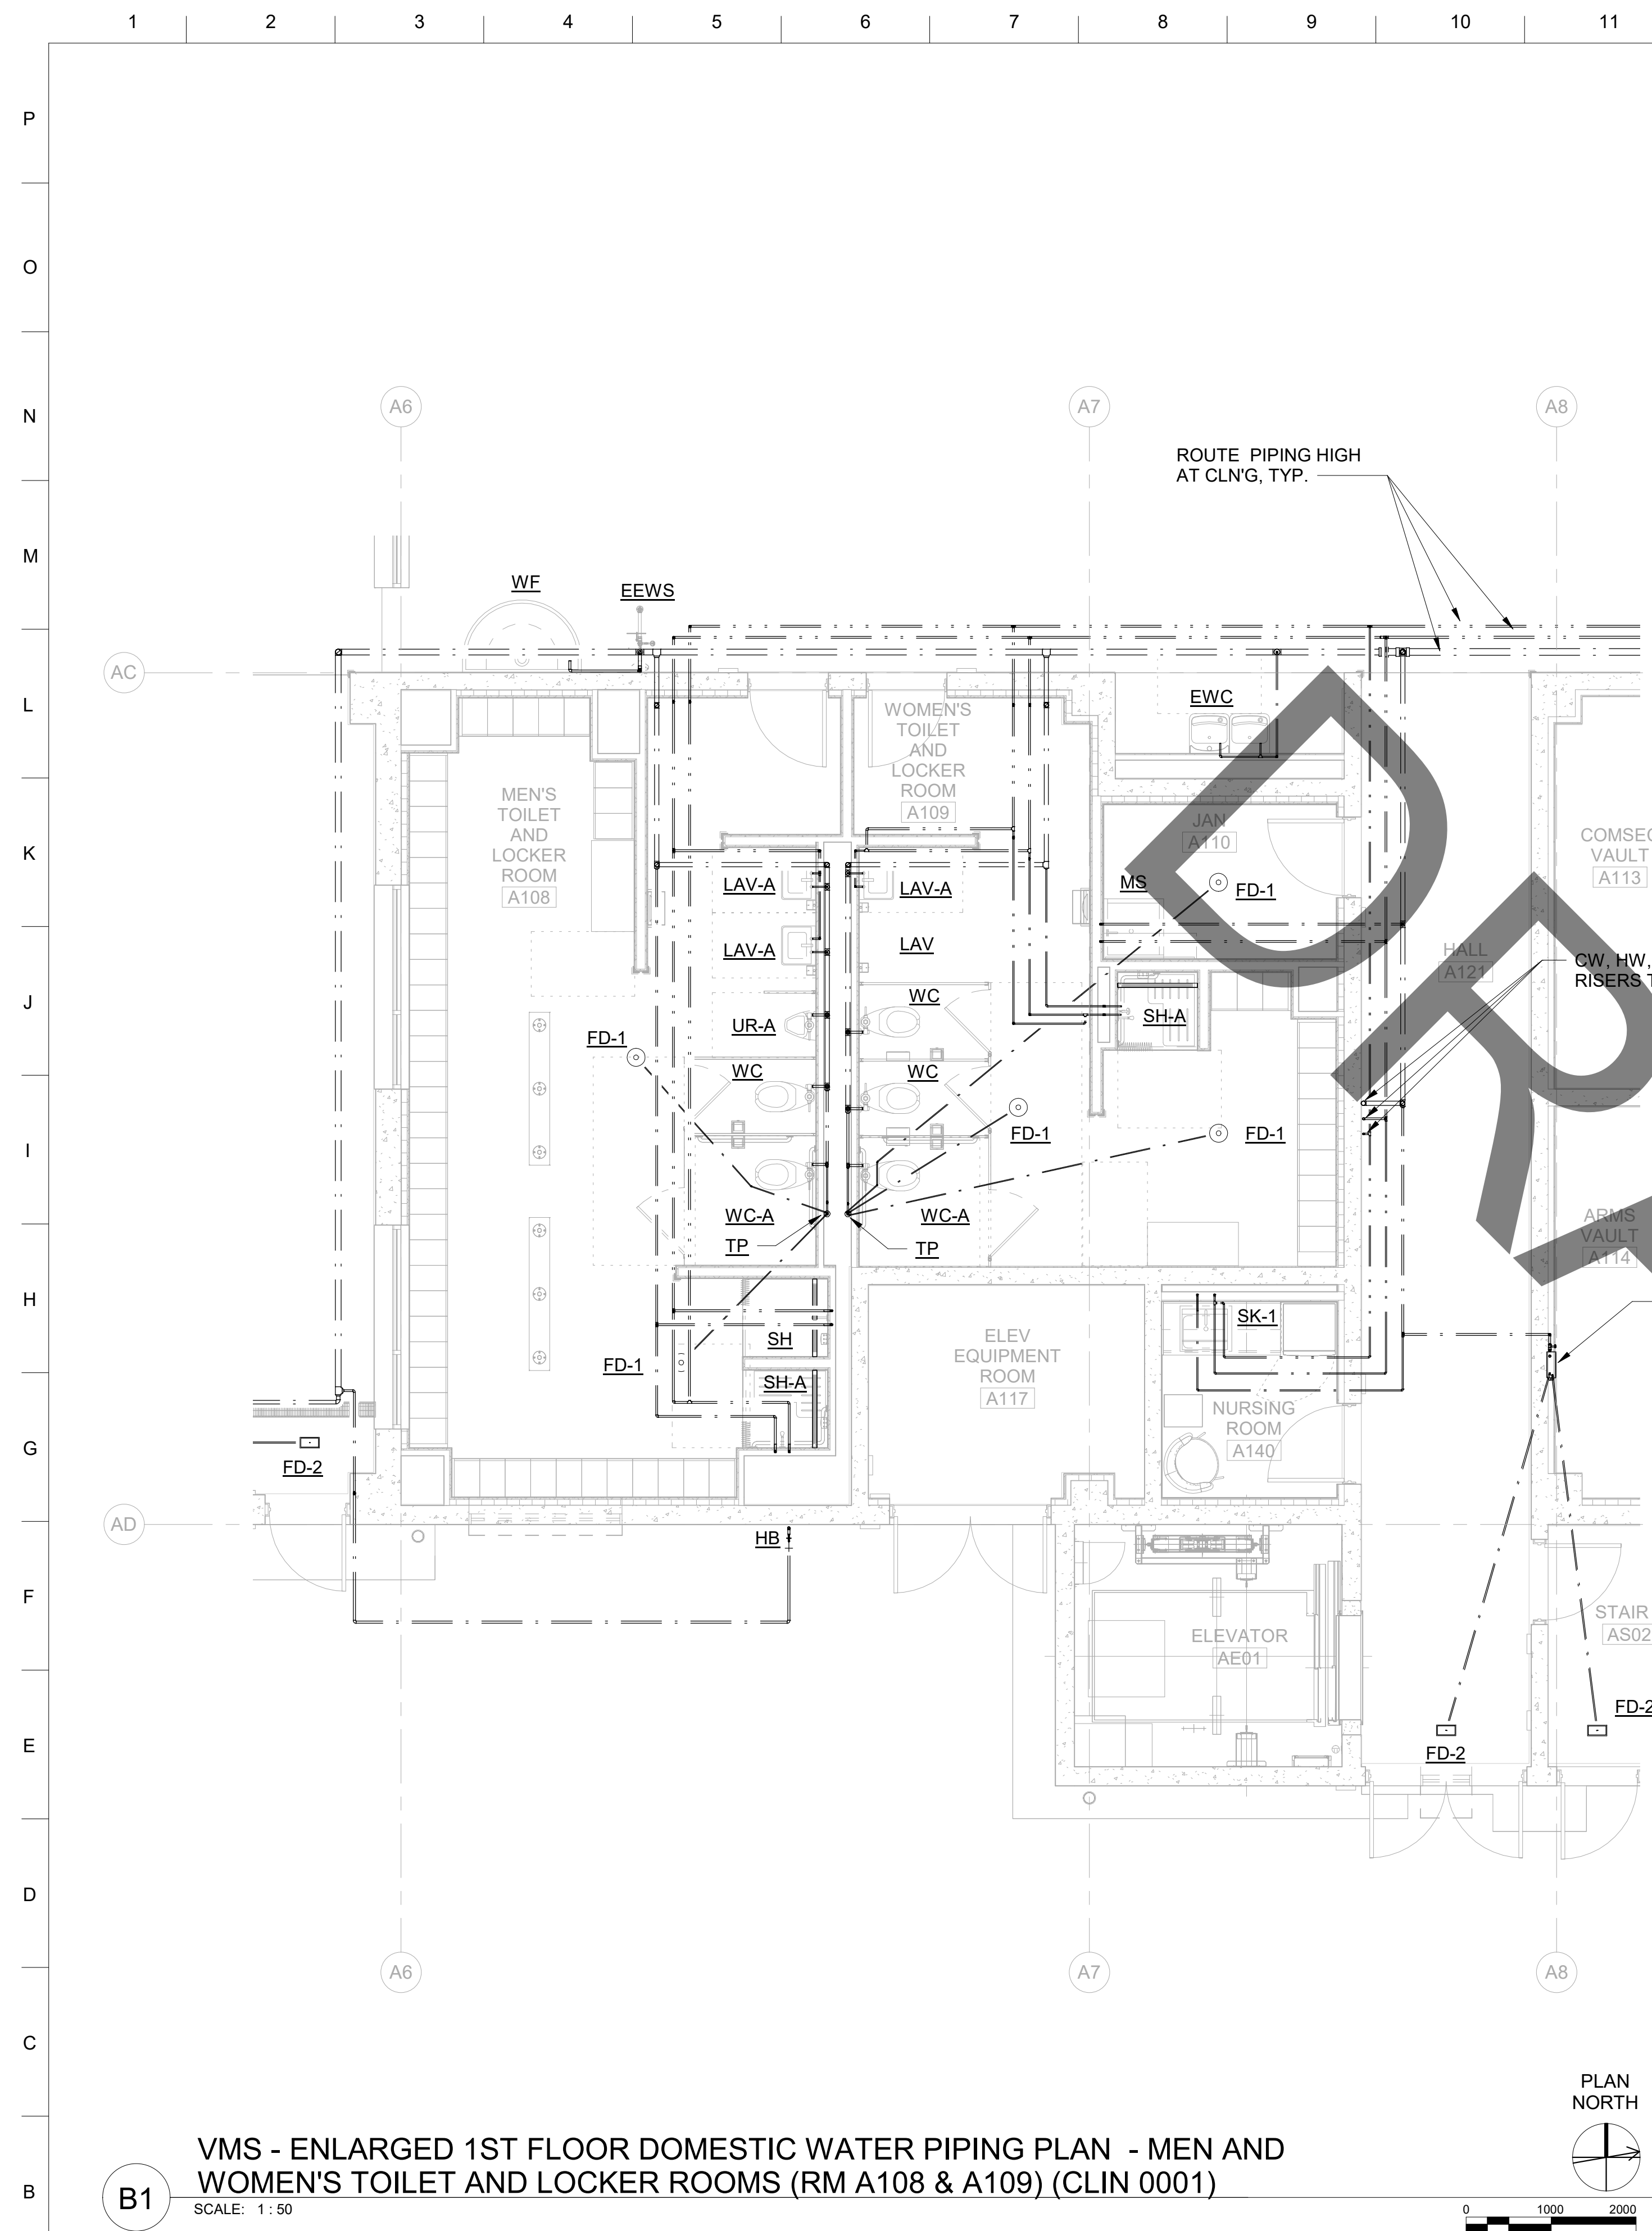

US Army Corps
of Engineers®[illegible]

US ARMY CORPS OF ENGINEERS JAPAN ENGINEER DISTRICT OKINAWA AREA OFFICE APO AP 96376-5132	DESIGNED BY: I. TSANG	ISSUE DATE:
DESIGN PARTNERS, INCORPORATED 1500 HAKOLA STREET, SUITE 1100 HONOLULU, HAWAII 96814	DRAWN BY: R. BALIGNASAY	SOLICITATION NO.:
	CHECKED BY: O. CRABTREE	CONTRACT NO.:
	SUBMITTED BY:	W912HV-17-D-0003
	SIZE:	

FY20 MCA PN77833 VEHICLE MAINTENANCE SHOP
KADENA AIR BASE, OKINAWA, JAPAN

VMS - ENLARGED DOMESTIC WATER PIPING
PLAN (CLIN 0001)


SHEET ID

P-A402

INTERMEDIATE DESIGN


Plot Date: 12/15/2025 1:19:09 PM File Path:

NAME	DESCRIPTION
C:\Users\rbalignasay\Documents\511758_TEMF_PLUMB_v2022_rbalgignasay.rv	

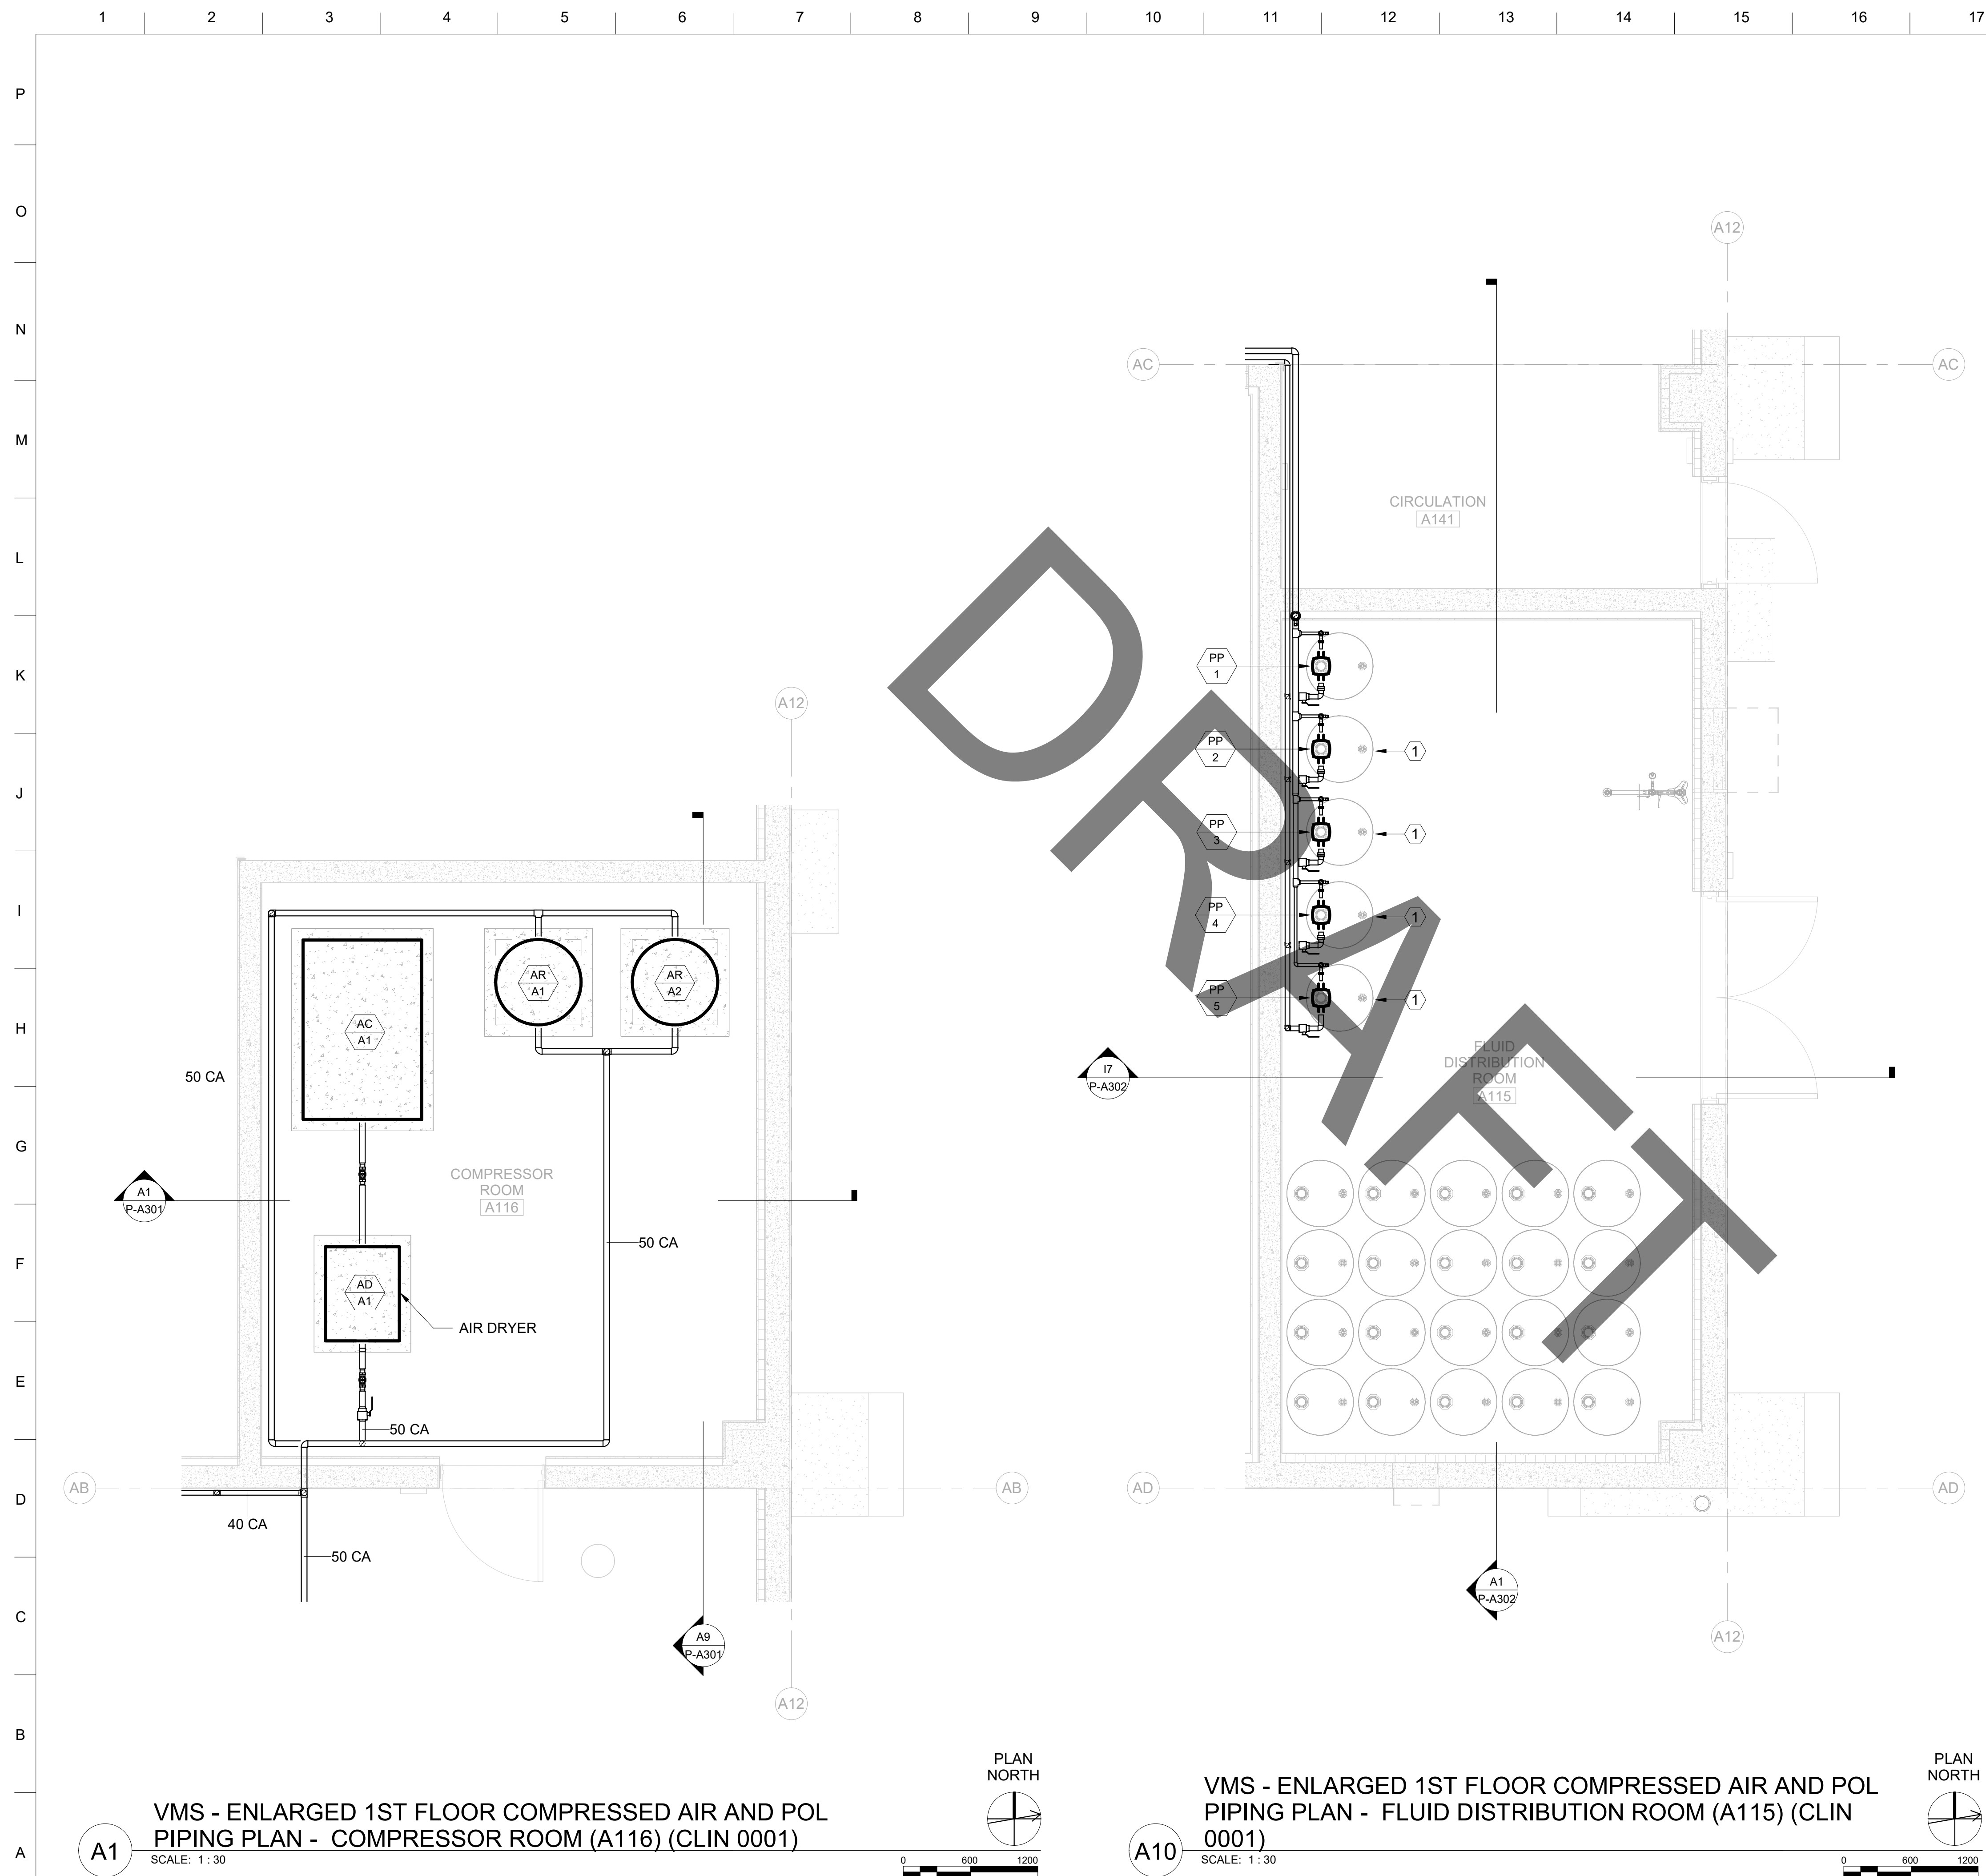

KEY NOTES

1 ANTI-FREEZE, GEAR OIL, ENGINE OIL, TRANSMISSION FLUID, AND GREASE DRUMS, TYPICAL.

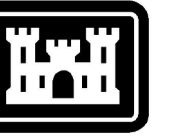

US Army Corps
of Engineers®

[illegible]

US ARMY CORPS OF ENGINEERS JAPAN ENGINEER DISTRICT OKINAWA AREA APO AP 96376-5132	DESIGNED BY:	ISSUE DATE:
	DRAWN BY:	SOLICITATION NO.:
	CHECKED BY:	CONTRACT NO.:
DESIGN PARTNERS INCORPORATED 1580 MAKALOA TRAIL, SUITE 1100 HONOLULU, HAWAII 96814	SUBMITTED BY: SIZE: ANSI D	W912H5-17-D-0003

FY20 MCA PN77833 VEHICLE MAINTENANCE SHOP
KADENA AIR BASE, OKINAWA, JAPAN

VMS - ENLARGED 1ST FLOOR COMPRESSED
AIR AND POL PIPING PLAN (CLIN 0001)

SHEET ID



P-A403

CLIN 0001

INTERMEDIATE DESIGN

Plot Date: 12/15/2025 1:19:12 PM File Path:

C:\Users\rballignasay\Documents\511758_TEMF_PLUMB_v2022_rballignasay.rvt

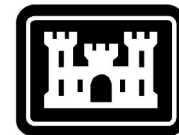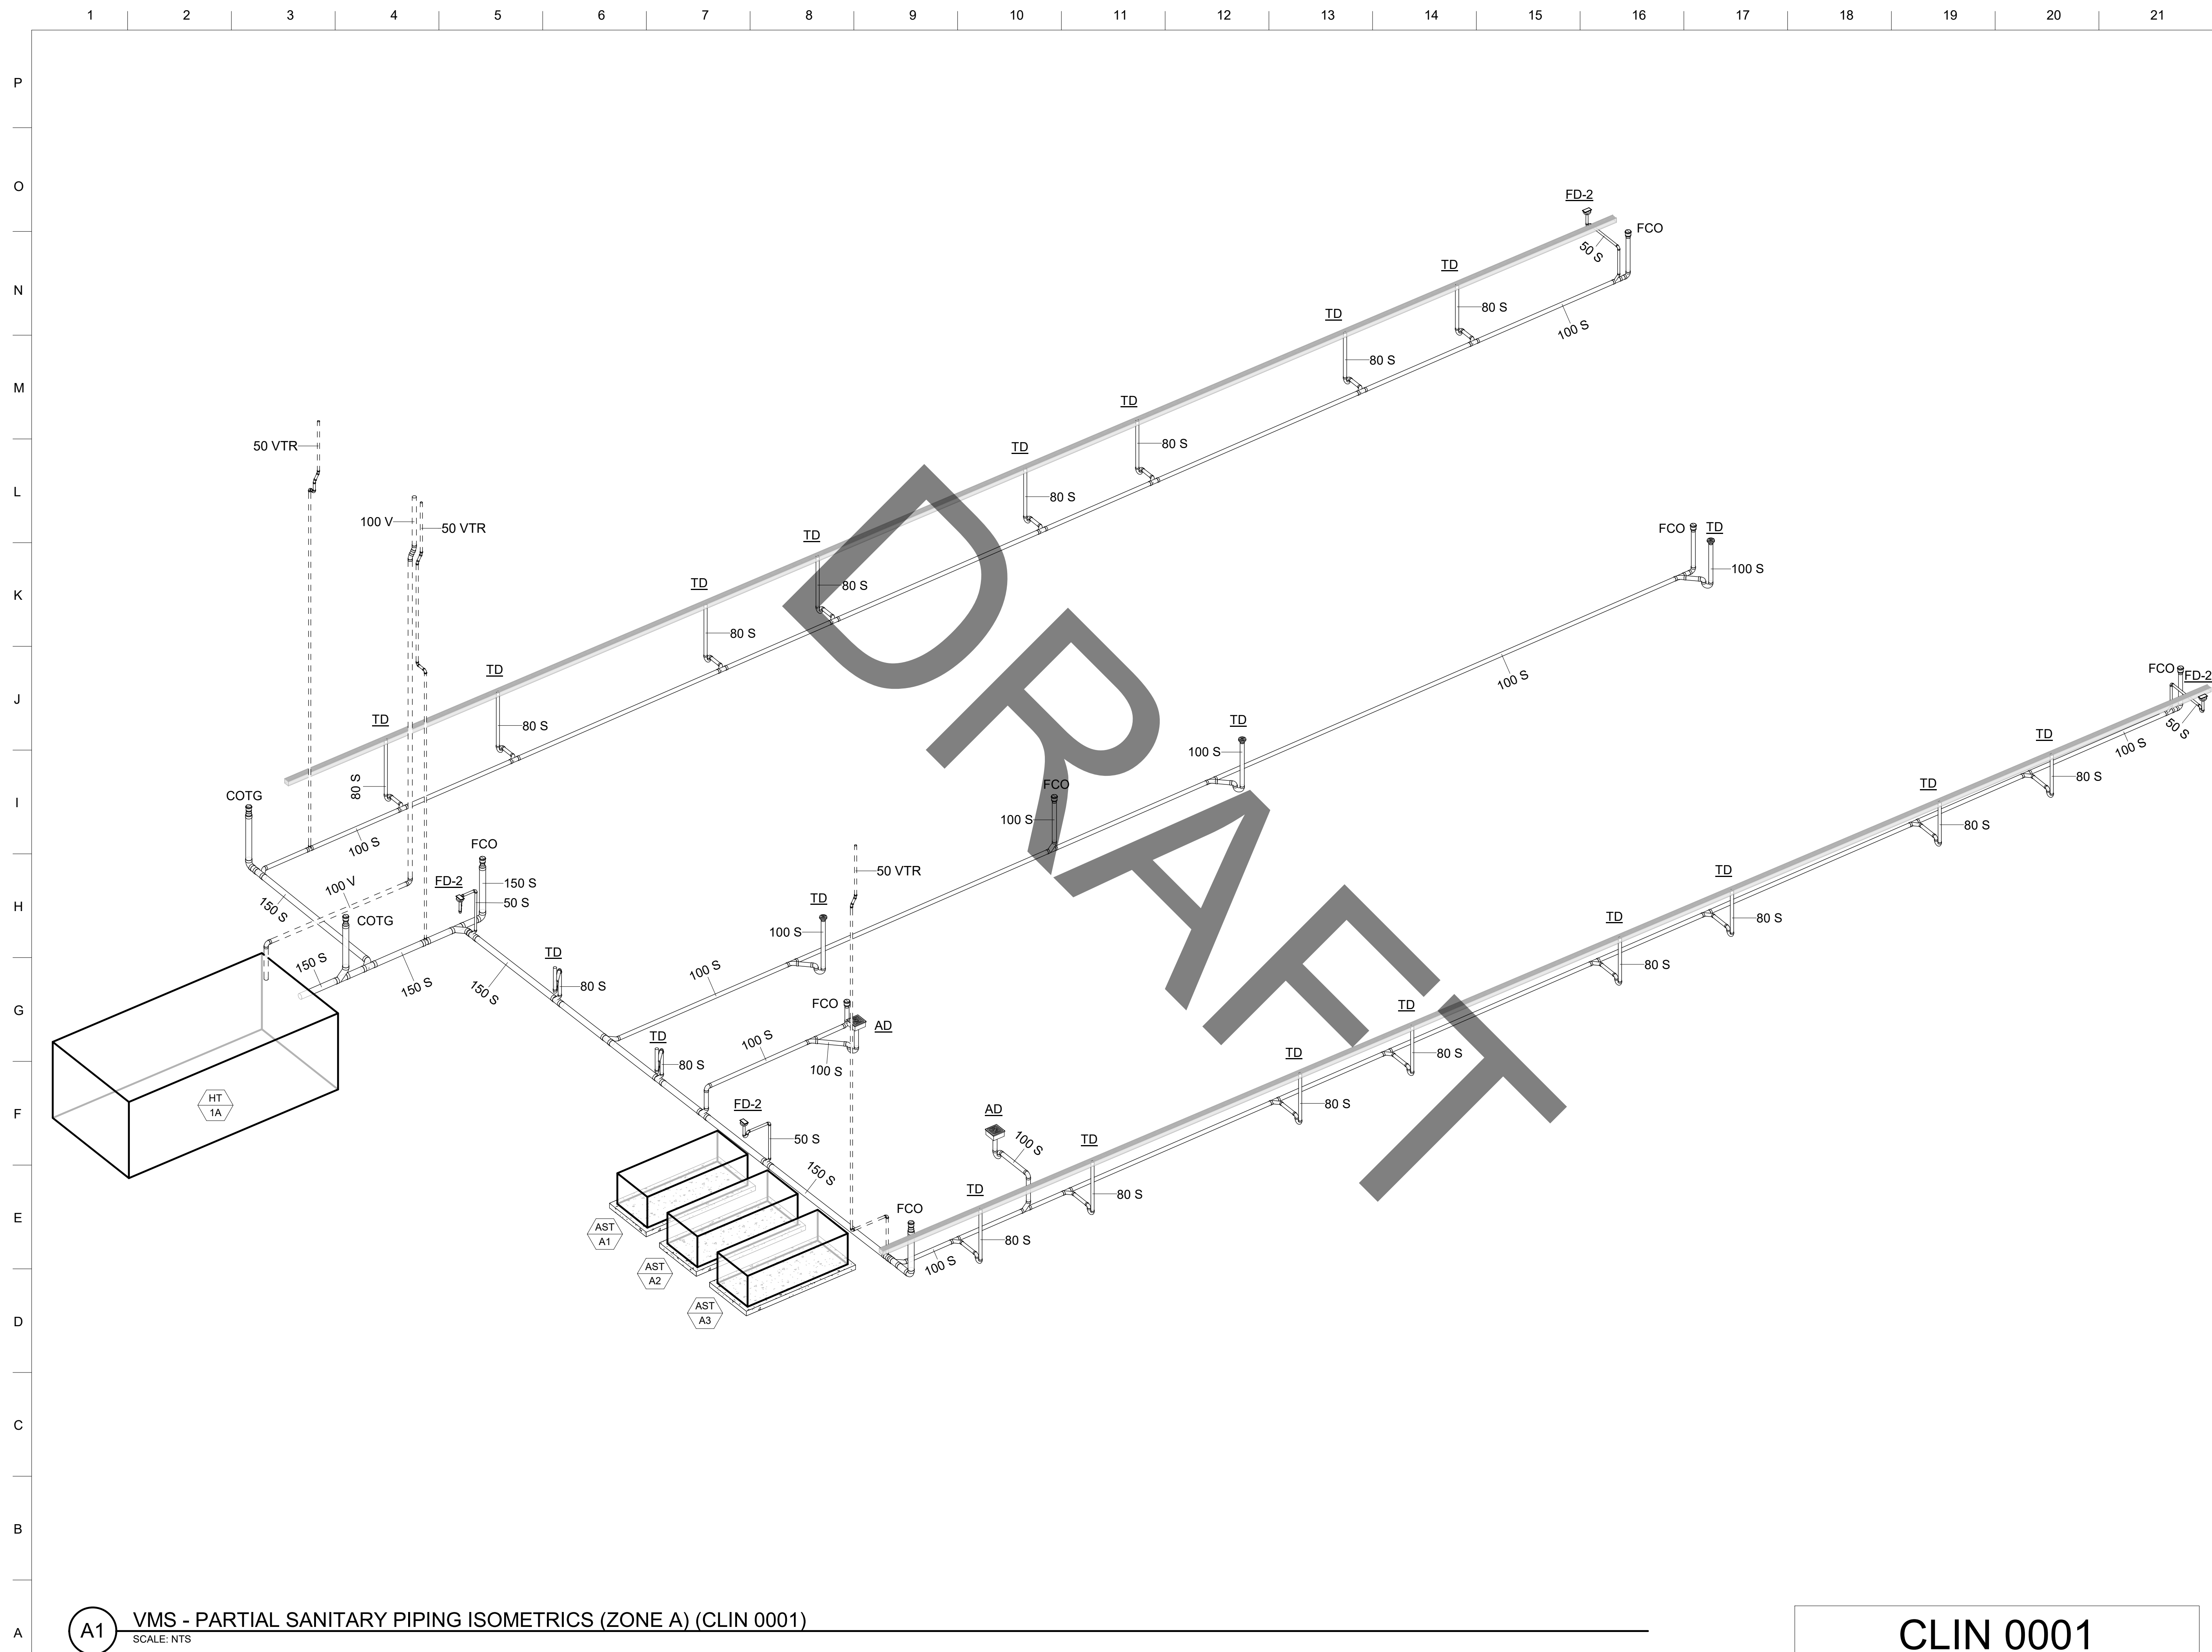

**US Army Corps
of Engineers ®**

[illegible]

US ARMY CORPS OF ENGINEERS JAPAN ENGINEER DISTRICT OKINAWA AREA OFFICE APO AF 96376-5132	DESIGNED BY: I. TSANG R. BALIGNASAY	ISSUE DATE:
DESIGN PARTNERS INCORPORATED 1580 MAKALOA STREET, SUITE 1100 HONOLULU, HAWAII 96814	CHECKED BY: O. CRASTREE SUBMITTED BY:	SOLICITATION NO.: CONTRACT NO.: W812HW-17-D-0003
	SIZE: ANSI/D	

FY20 MCA PN7833 VEHICLE MAINTENANCE SHOP
 KADENA AIR BASE, OKINAWA, JAPAN

SHEET ID

P-A901

C:\Users\rbalignasay\Documents\511758_TEMF_PLUMB_v2022_rbalignasay.rvt

File Path:

Plot Date: 12/15/2025 1:19:19 PM

INTERMEDIATE DESIGN

