



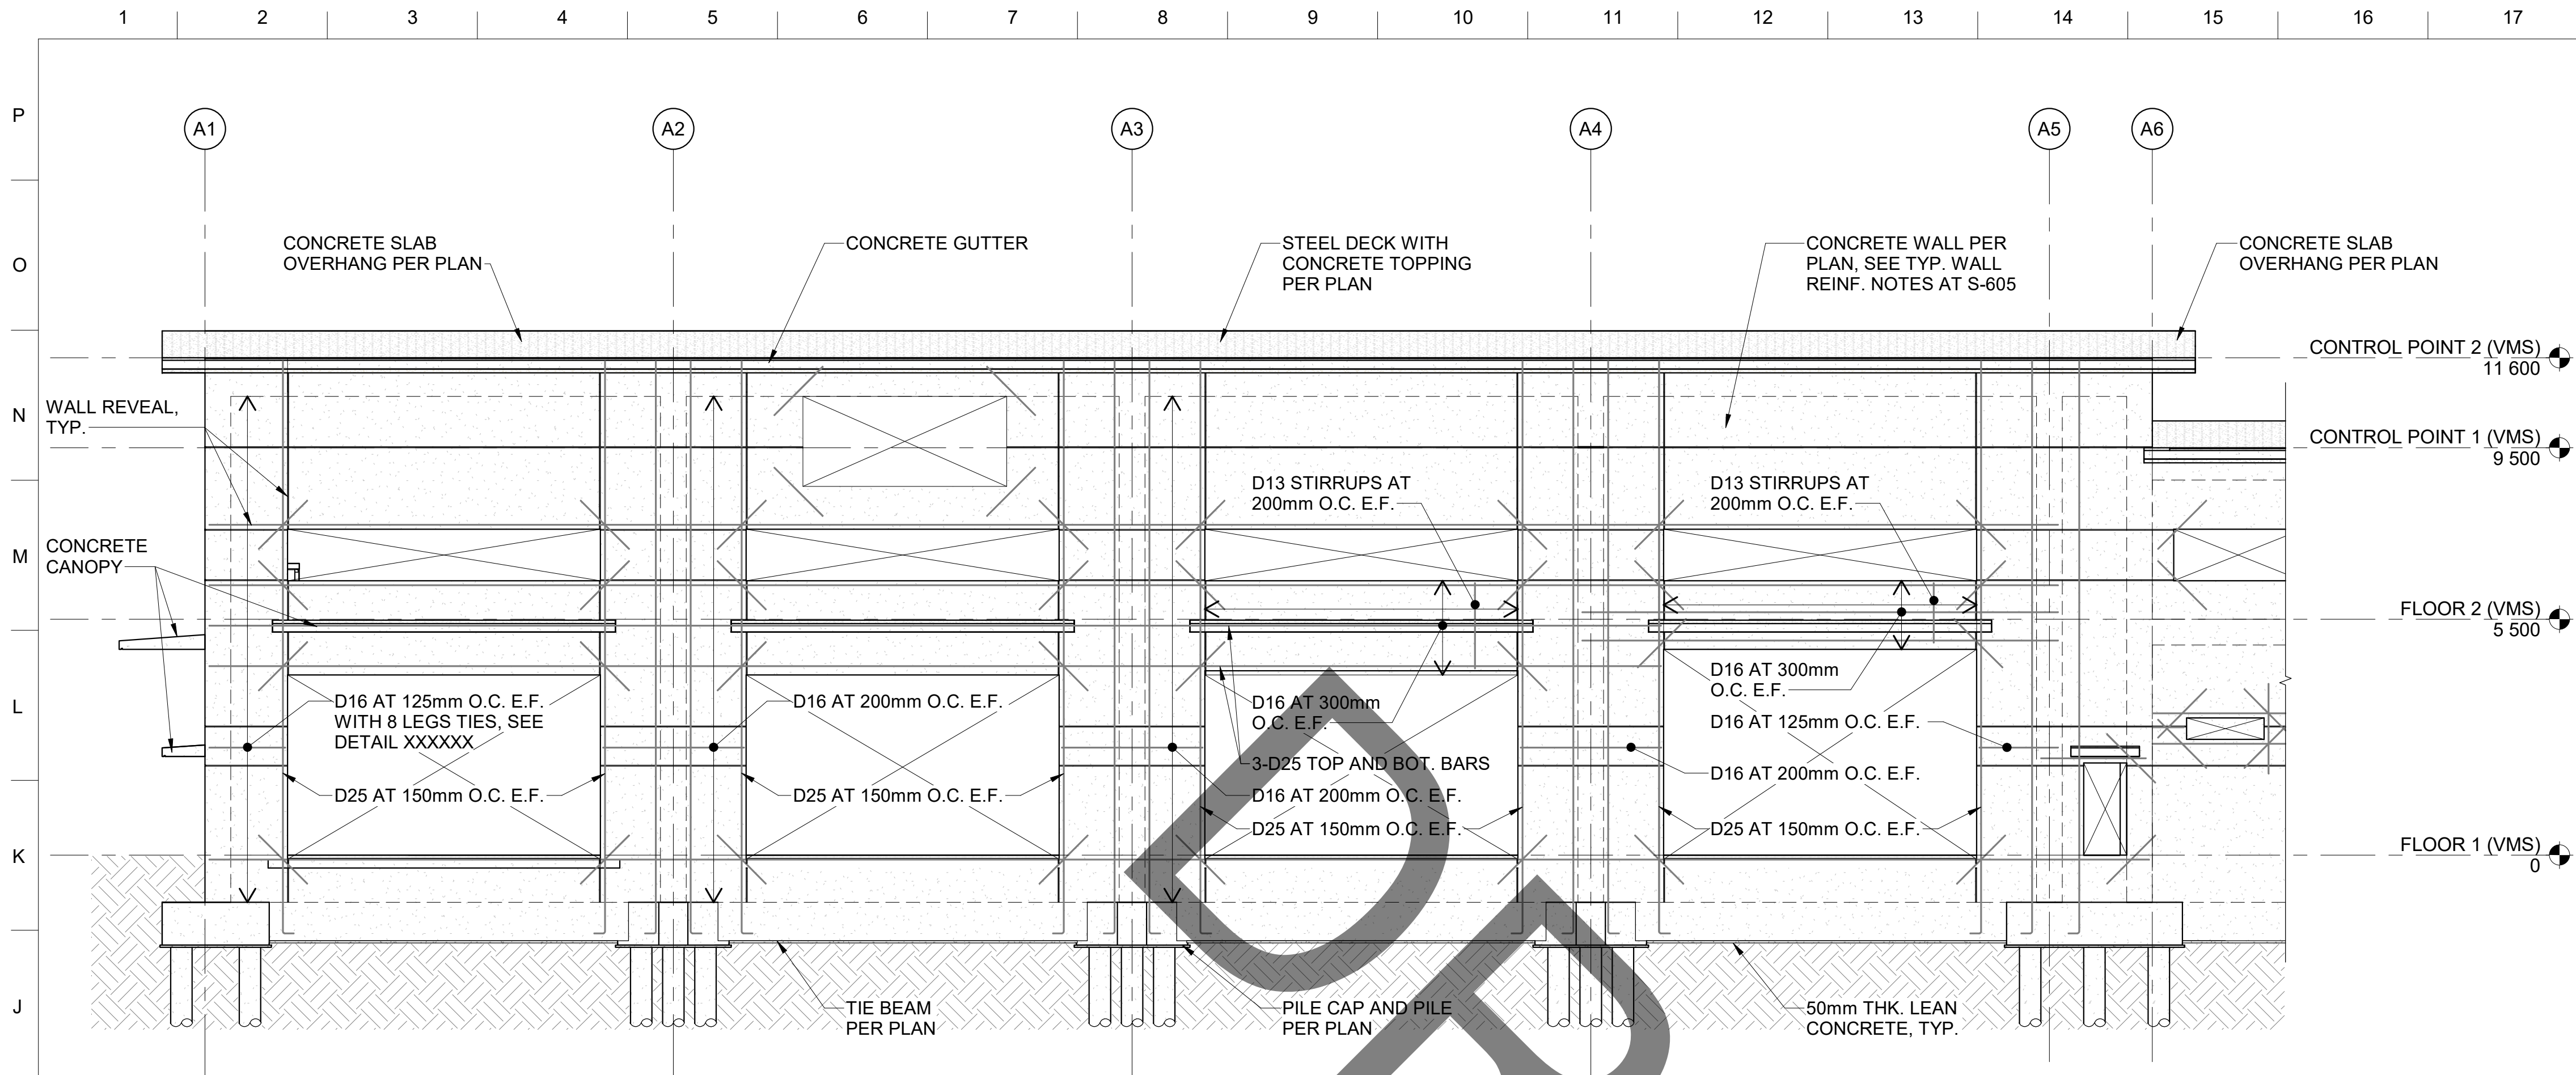

I1 VMS - EXTERIOR ELEVATION (SOUTH) (CLIN 0001)
SCALE 1 : 100

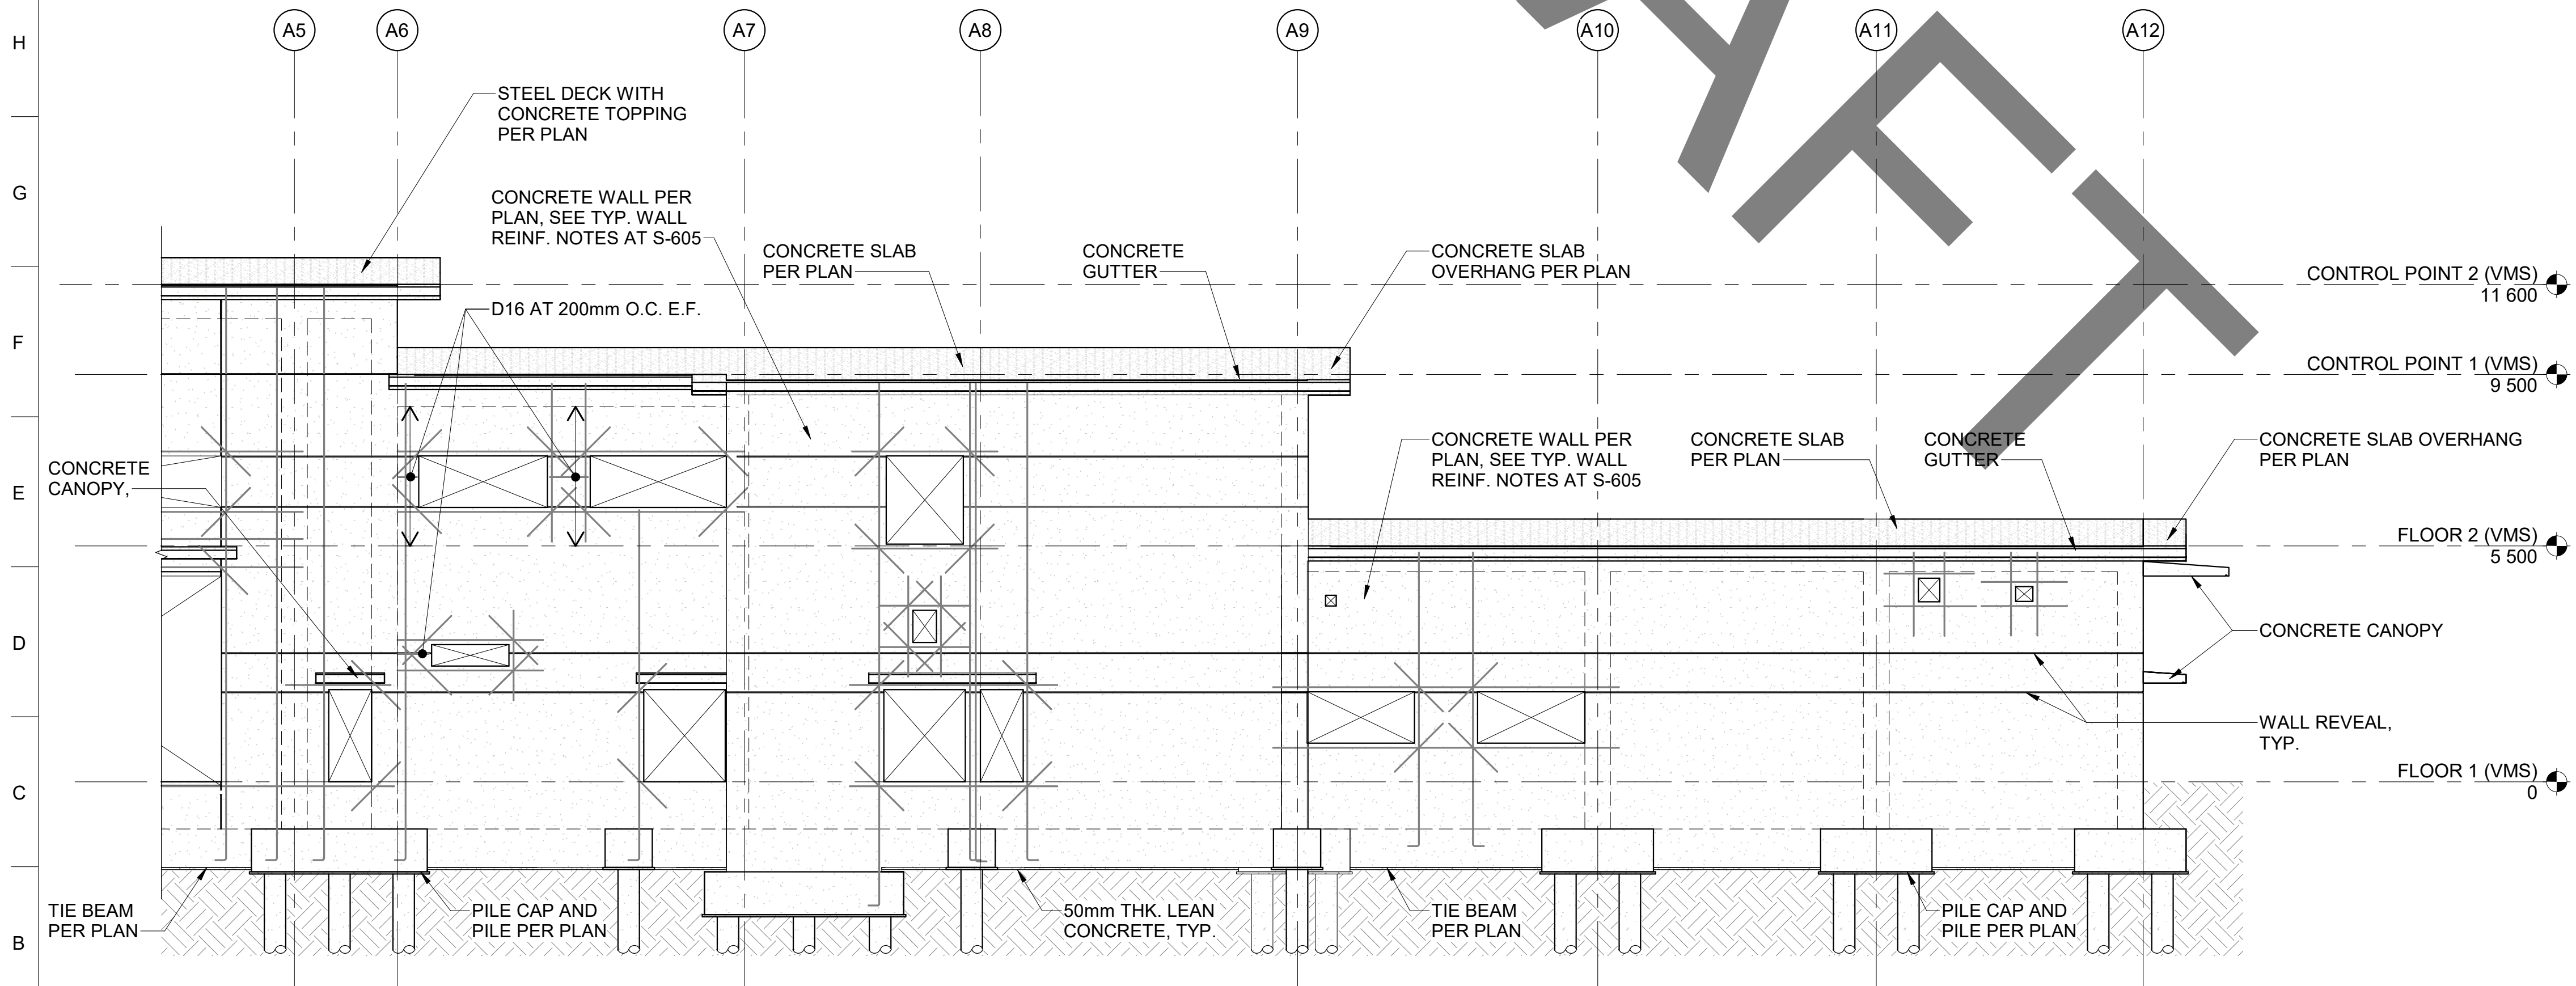

A1 VMS - EXTERIOR ELEVATION (SOUTH CONT.) (CLIN 0001)
SCALE 1 : 100

REFERENCE DRAWINGS



- S-001 - GENERAL NOTES
- S-002 - DESIGN DATA, DESIGN CODES AND STANDARDS, ABBREVIATION
- S-501 - TYPICAL REINFORCING STEEL DETAILS
- S-601 - CONCRETE PILE CAP SCHEDULE
- S-602 - CONCRETE PILE SCHEDULE
- S-603 - CONCRETE GRADE BEAM AND TIE BEAM SCHEDULE
- S-605 - CONCRETE WALL SCHEDULE
- S-606 - CONCRETE COLUMN SCHEDULE
- S-607 - CONCRETE BEAM SCHEDULE
- S-A601 - TRUSS DETAILS

NOTES

- SEE ARCHITECTURAL DRAWINGS FOR DIMENSIONS, ELEVATIONS AND DETAILS NOT SHOWN ON STRUCTURAL DRAWINGS.
- SEE ARCHITECTURAL DRAWINGS FOR FLOOR SLOPE.
- VERIFY WITH ARCHITECT/MECHANICAL FOR SIZE AND LOCATION OF OPENINGS.

CLIN 0001

GRAPHIC SCALE

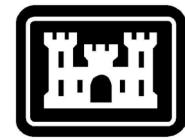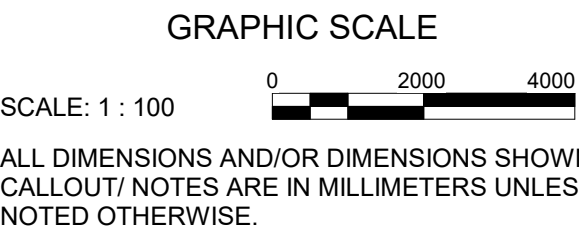

US Army Corps
of Engineers ®

MARK	DESCRIPTION	DATE

DESIGNED BY: J. RABANAL	ISSUE DATE: JUNE 2018
DRAWN BY: R. TANGONAN	SOLICITATION NO.: W912AV-17-D-0003
CHECKED BY: J. JUNG	CONTRACT NO.: W912AV-17-D-0003
SUBMITTED BY: J. JUNG	SIZE: ANSI D
US ARMY CORPS OF ENGINEERS JAPAN ENGINEER DISTRICT OKINAWA AREA OFFICE APO AP 96376-5132 SSFM SSFM INTERNATIONAL, INC. 507 SUMNER STREET, SUITE 620 HONOLULU, HAWAII 96817	

APO AP 96343-5010 FY20 MCA PN77833 VEHICLE MAINTENANCE SHOP VMS - EXTERIOR ELEVATIONS (CLIN 0001)


SHEET ID VMS S-A203

Autodesk Docs / Vehicle Maint Shop Kadena511736_TEMPL-STRUC.rvt



File Path:

Plot Date: 12/16/2025 3:35:50 PM

INTERMEDIATE DESIGN

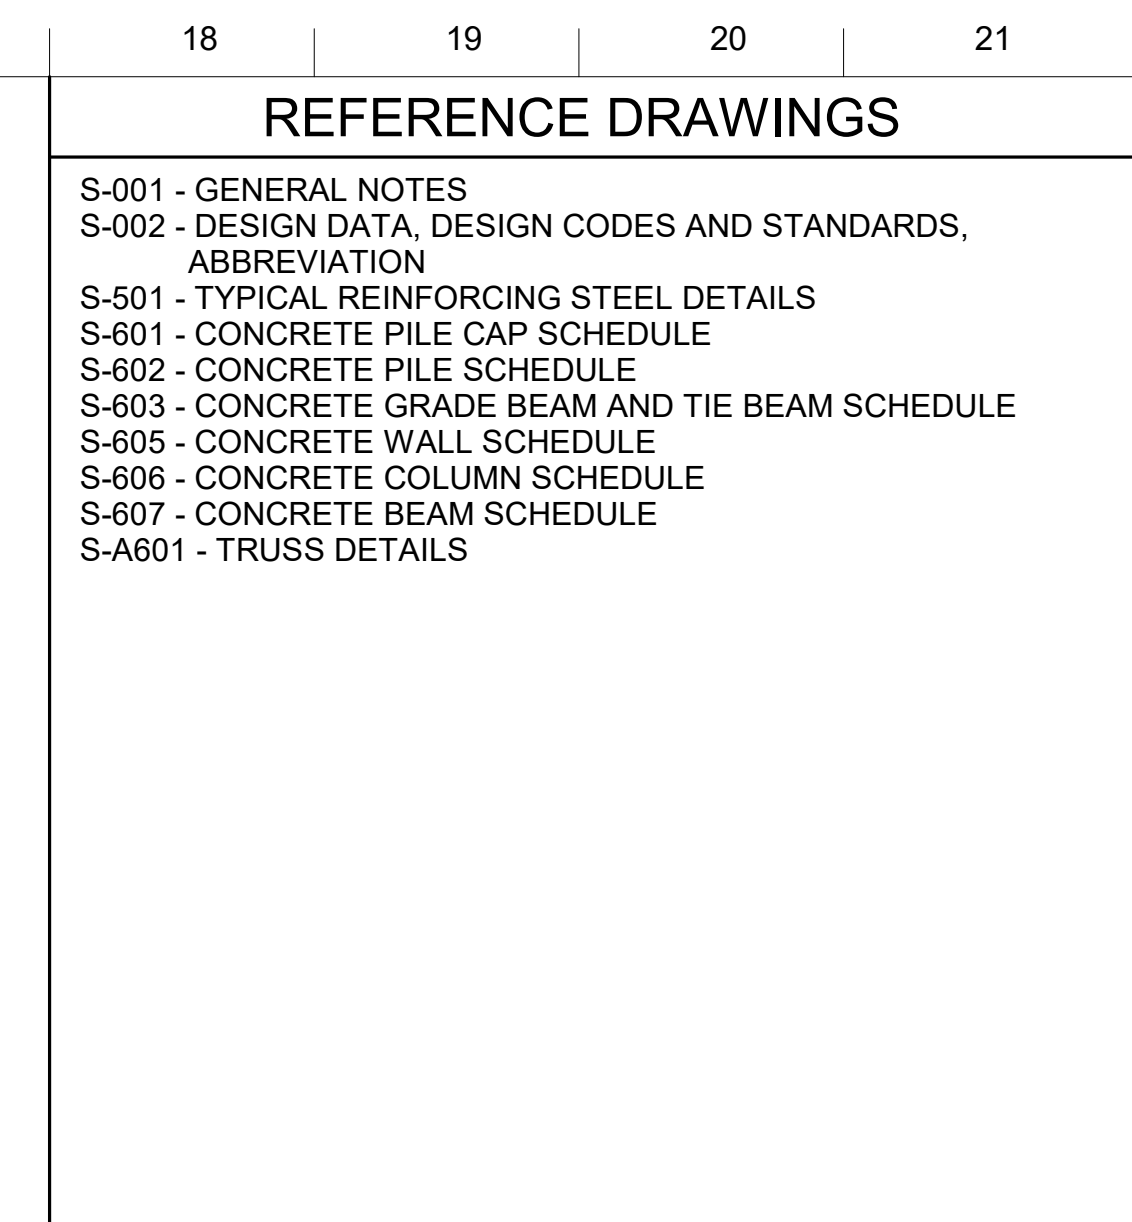

NOTES	
1.	SEE ARCHITECTURAL DRAWINGS FOR DIMENSIONS,

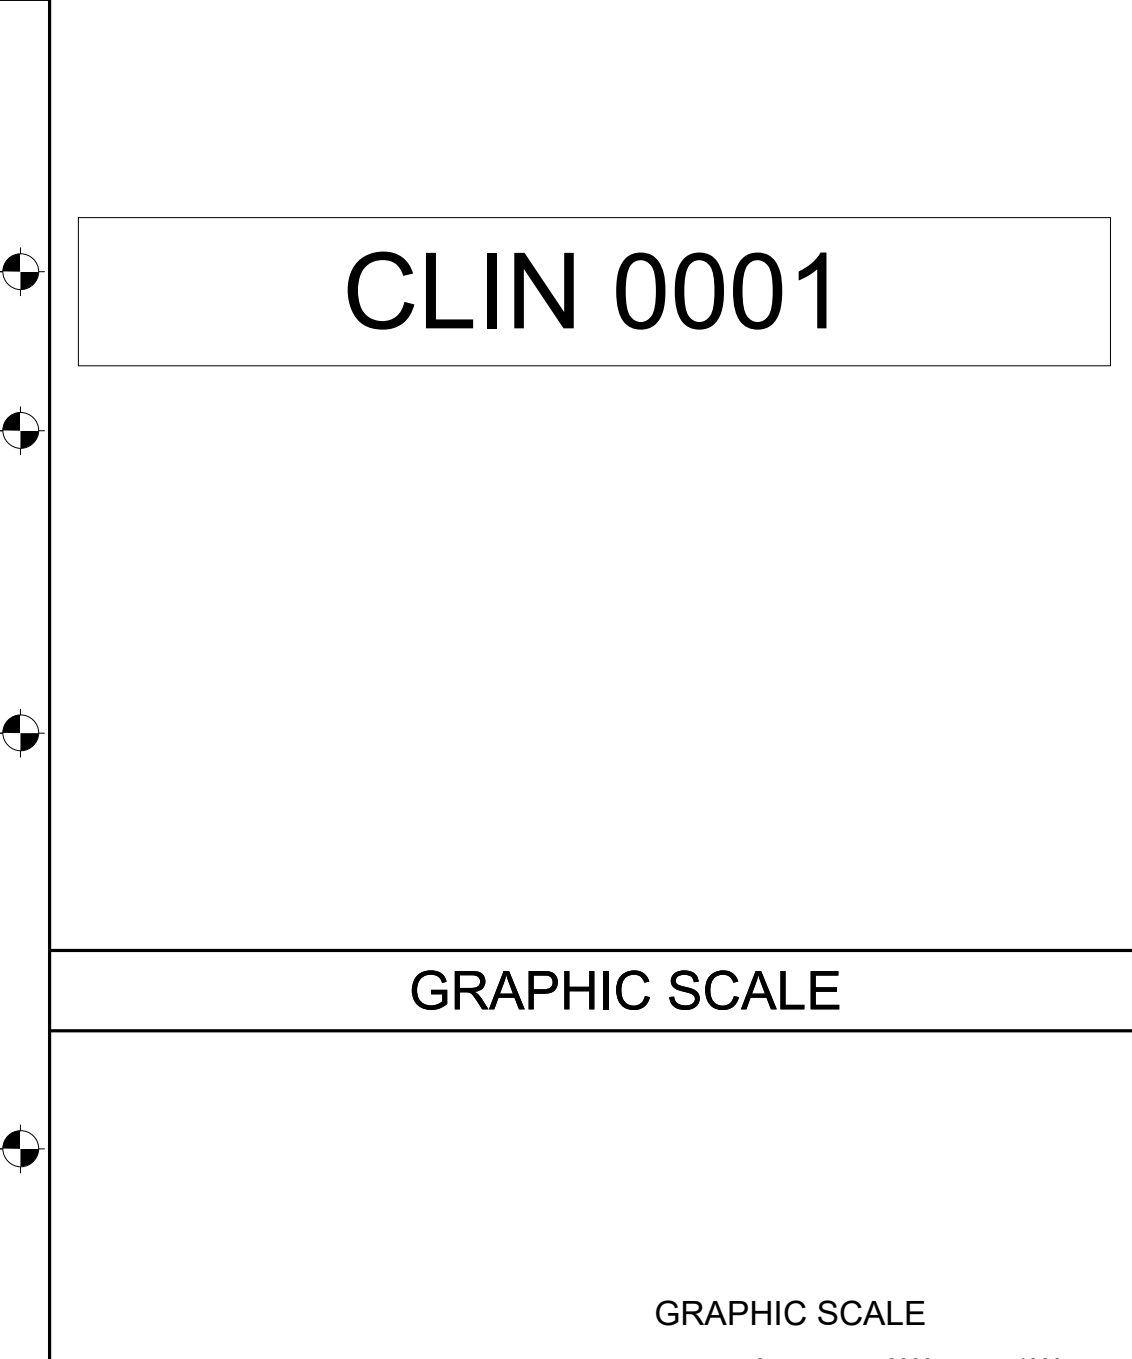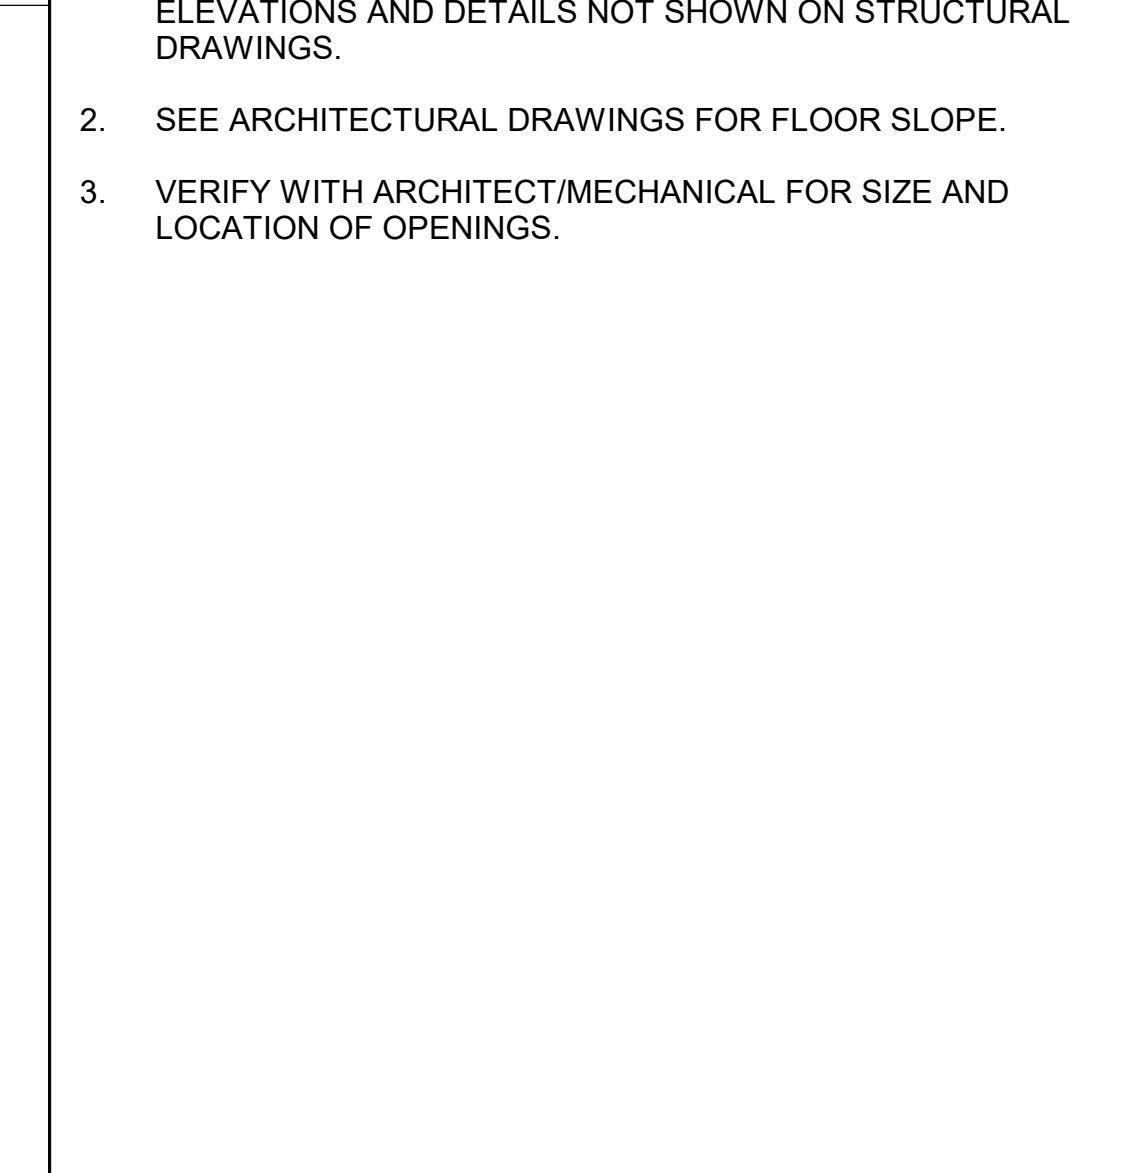


SCALE: 1 : 100


ALL DIMENSIONS AND/OR DIMENSIONS SHOWN IN
CALLOUT/NOTES ARE IN MILLIMETERS UNLESS
NOTED OTHERWISE.

APO AP 96345-5010 FY20 MCA PN7833 VEHICLE MAINTENANCE SHOP VMS - BUILDING SECTIONS (CLIN 0001)		 US Army Corps of Engineers ®	
US ARMY CORPS OF ENGINEERS JAPAN ENGINEER DISTRICT OKINAWA AREA OFFICE APO AP 96376-5132		DESIGNED BY: J. RABANAL DRAWN BY: R. TANGONAN CHECKED BY: J. UNO SUBMITTED BY: J. UNO	
SSFM SSFM INTERNATIONAL, INC. 501 SUMNER STREET, SUITE 620 HONOLULU, HAWAII 98817		ISSUE DATE: JUNE 2018 SOLICITATION NO.: CONTRACT NO.: W912HIV-7-45-0003	
		MARK DESCRIPTION	
		DATE	

Plot Date: 12/16/2025 3:35:55 PM File Path: Autodesk Docs\Vehicle Maint Shop Kadena\S11759_TEM_5THUC.rvt

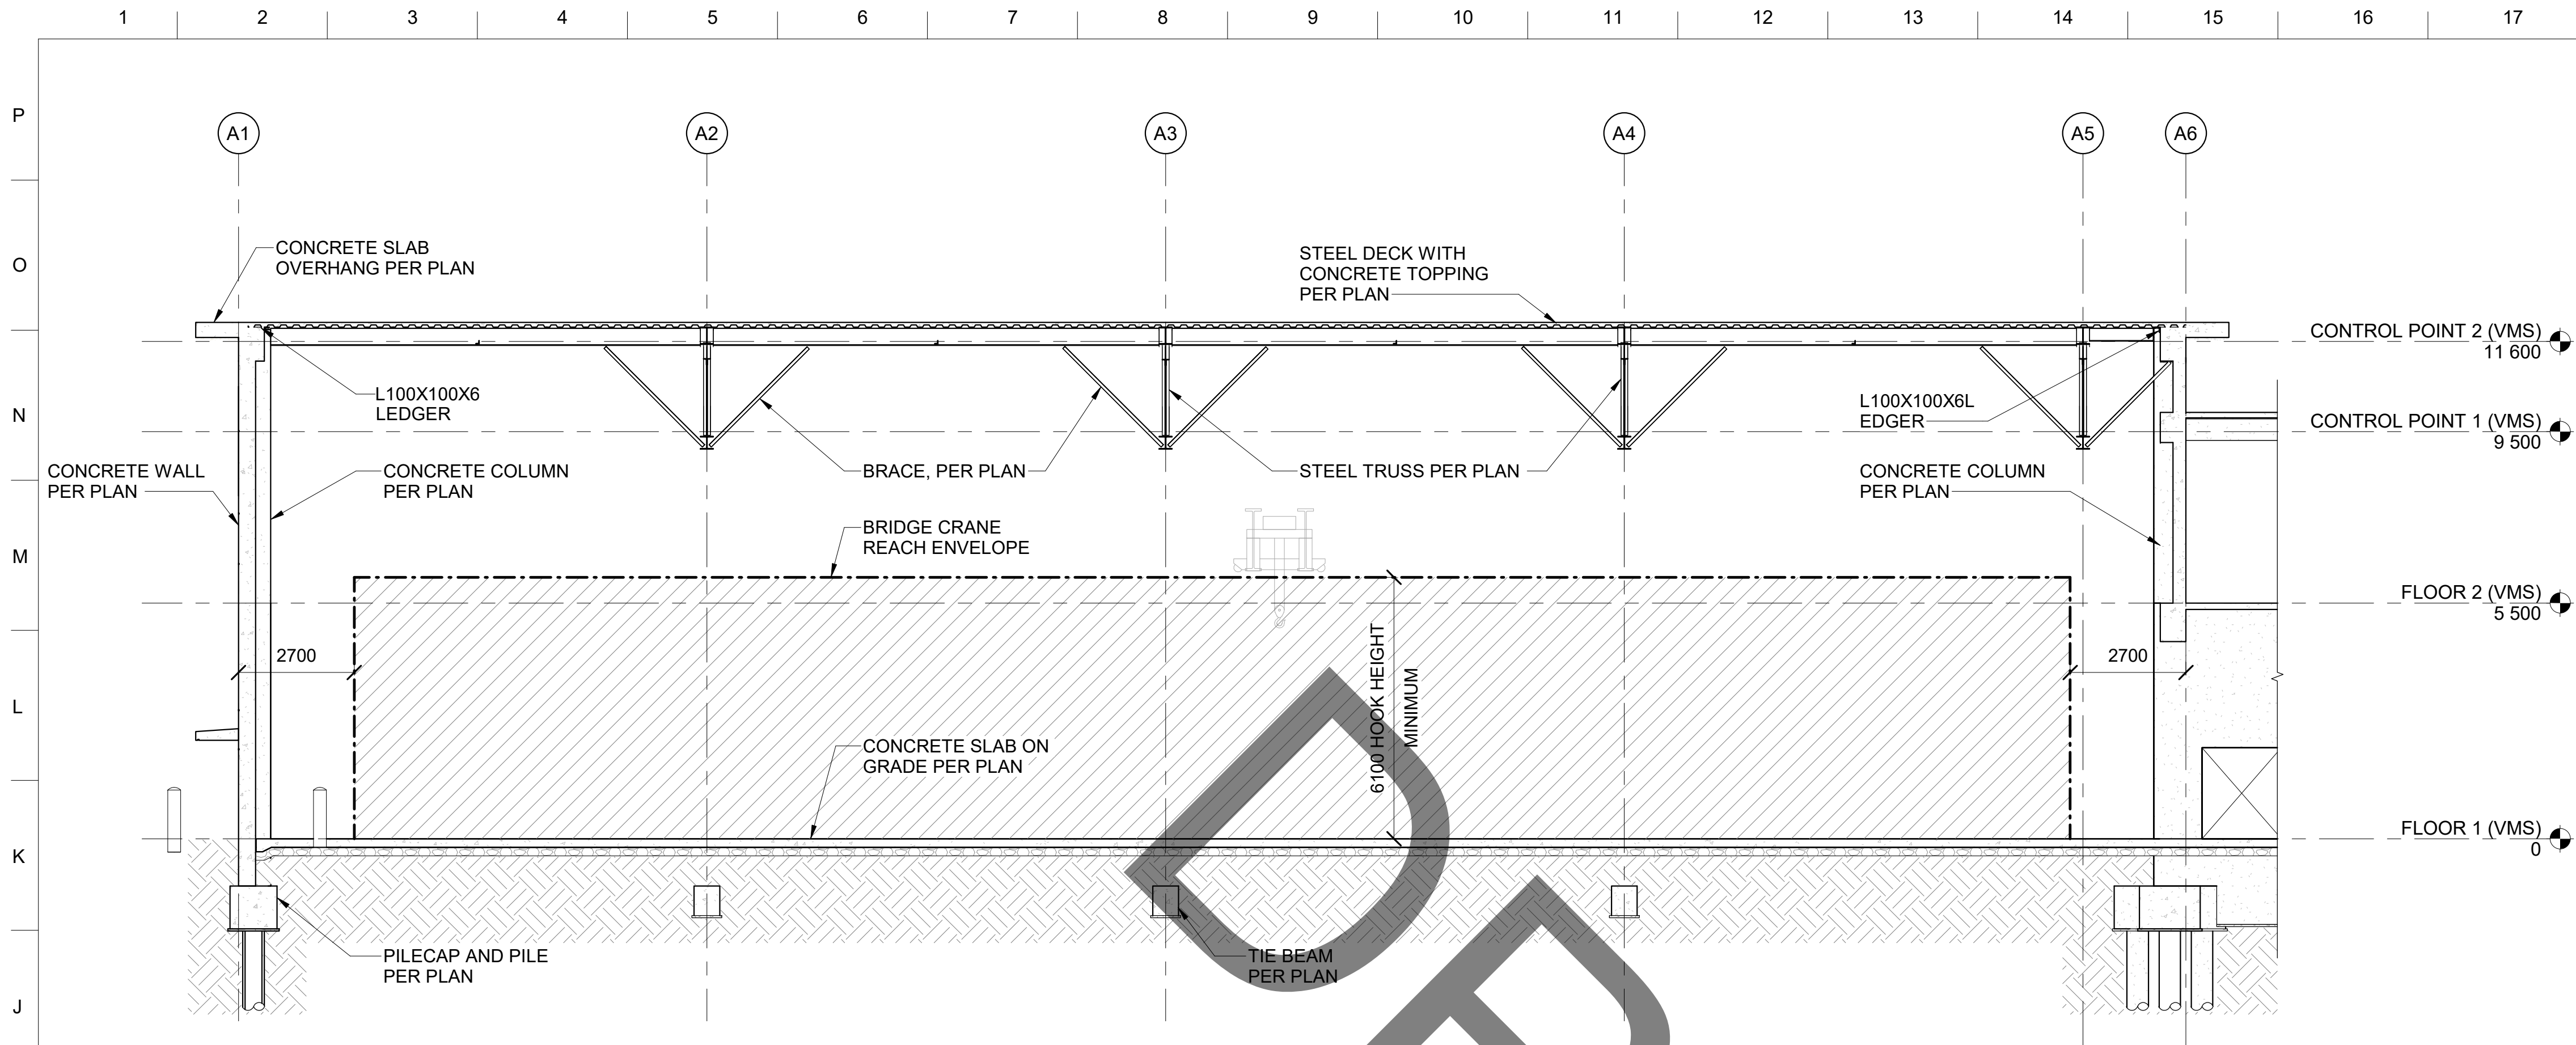

I1 VMS - BUILDING SECTION (CLIN 0001)
SCALE 1 : 100

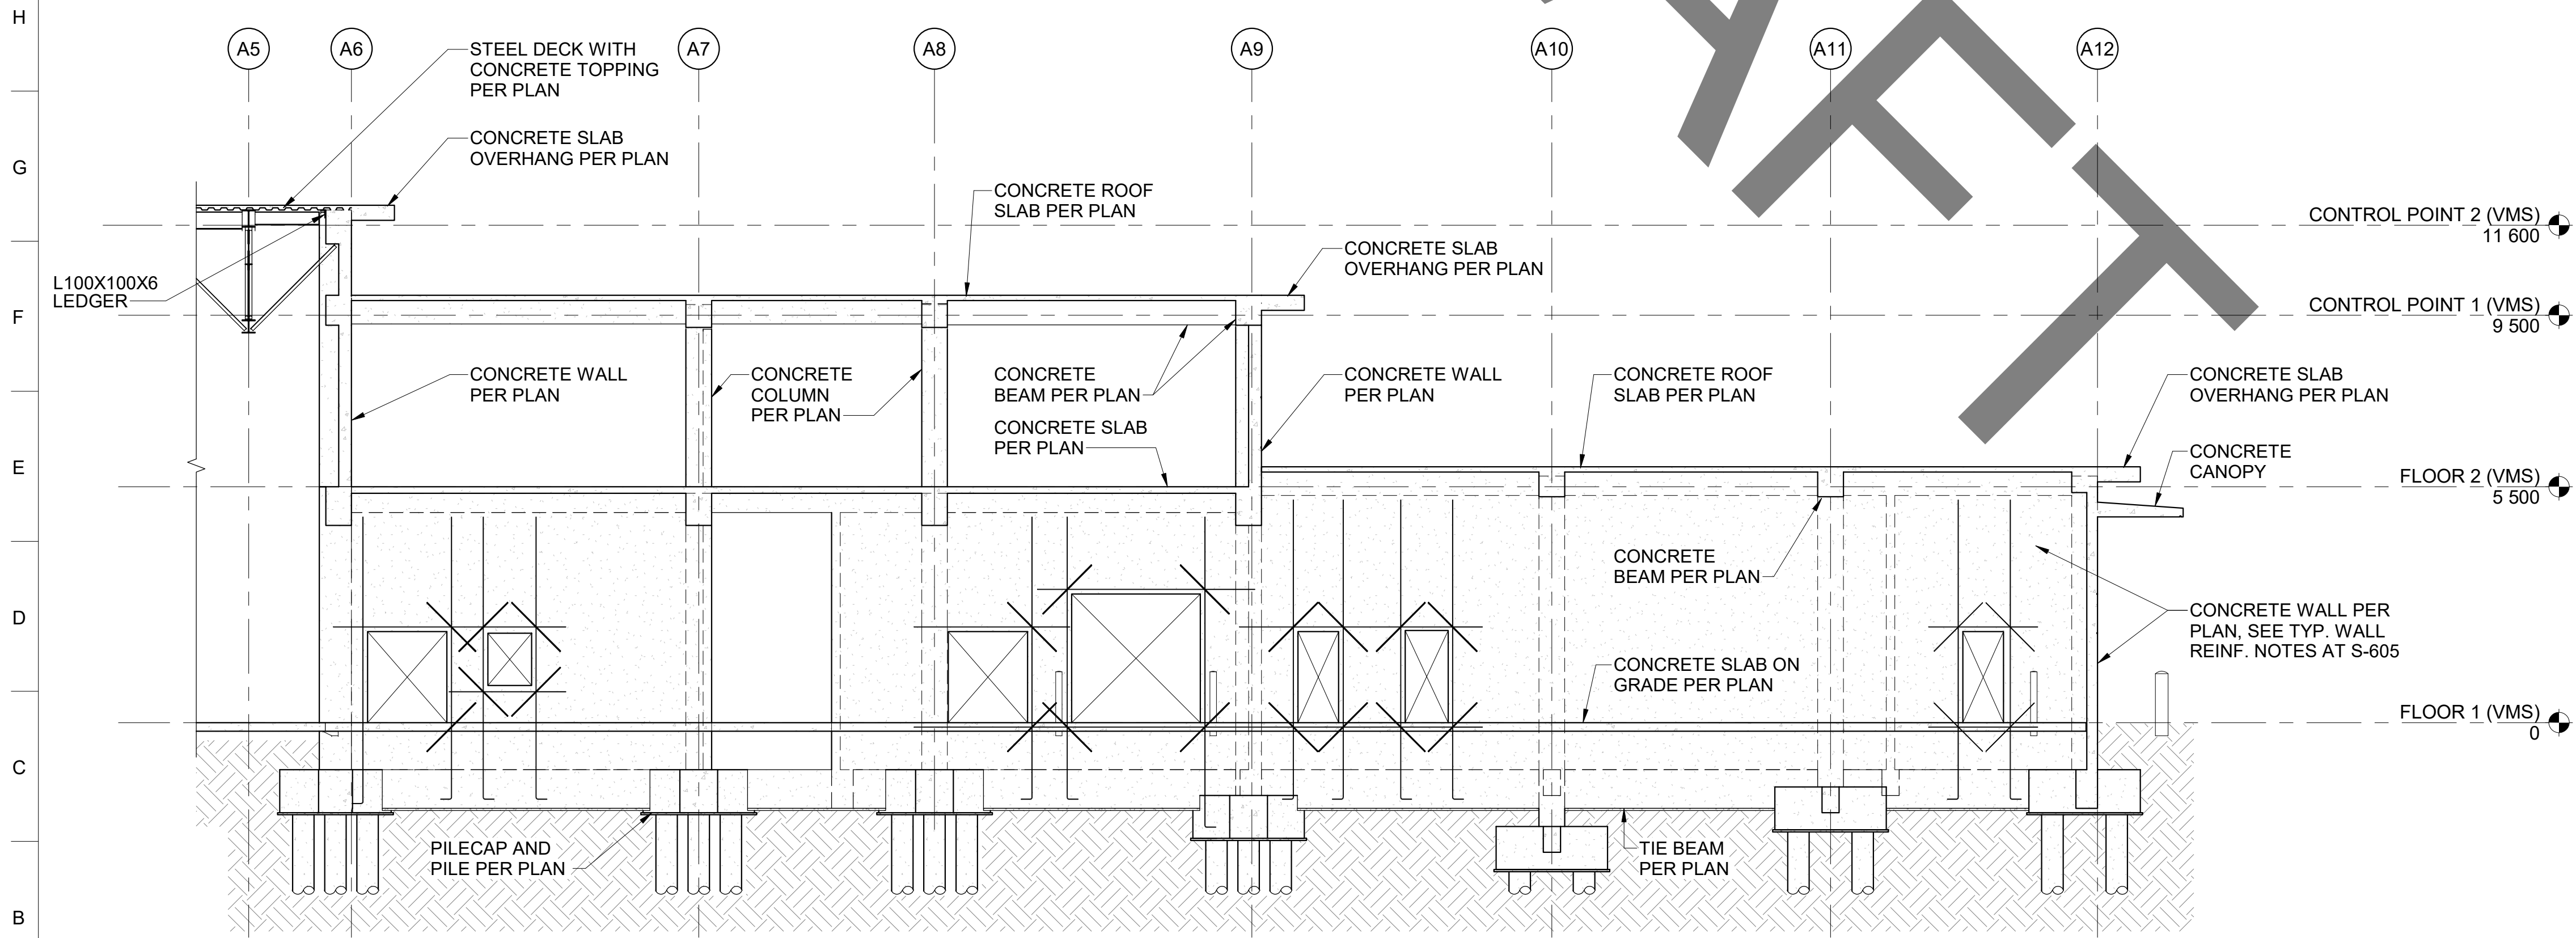

A1 VMS - BUILDING SECTION (CLIN 0001)
SCALE 1 : 100

REFERENCE DRAWINGS


- S-001 - GENERAL NOTES
- S-002 - DESIGN DATA, DESIGN CODES AND STANDARDS, ABBREVIATION
- S-501 - TYPICAL REINFORCING STEEL DETAILS
- S-601 - CONCRETE PILE CAP SCHEDULE
- S-602 - CONCRETE PILE SCHEDULE
- S-603 - CONCRETE GRADE BEAM AND TIE BEAM SCHEDULE
- S-605 - CONCRETE WALL SCHEDULE
- S-606 - CONCRETE COLUMN SCHEDULE
- S-607 - CONCRETE BEAM SCHEDULE
- S-A601 - TRUSS DETAILS

NOTES

- SEE ARCHITECTURAL DRAWINGS FOR DIMENSIONS, ELEVATIONS AND DETAILS NOT SHOWN ON STRUCTURAL DRAWINGS.
- SEE ARCHITECTURAL DRAWINGS FOR FLOOR SLOPE.
- VERIFY WITH ARCHITECT/MECHANICAL FOR SIZE AND LOCATION OF OPENINGS.

CLIN 0001

GRAPHIC SCALE

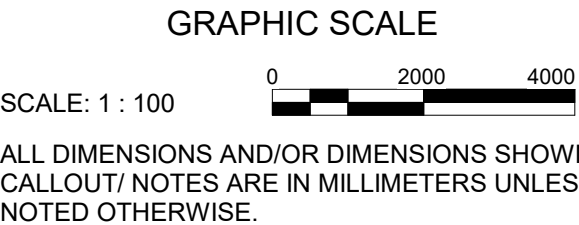

US Army Corps
of Engineers ®


MARK	DESCRIPTION	DATE

DESIGNED BY: J. RABANAL	ISSUE DATE: JUNE 2018
DRAWN BY: R. TANGONAN	SOLICITATION NO.:
CHECKED BY: J. LINO	CONTRACT NO.: W72WY-17-D-0003
SUBMITTED BY: 	
SIZE: ANSI D	

US ARMY CORPS OF ENGINEERS JAPAN ENGINEER DISTRICT OKINAWA AREA OFFICE APO AP 96376-5132	SSFM STRUCTURAL SSFM INTERNATIONAL, INC. 507 SUMNER STREET, SUITE 620 HONOLULU, HAWAII 96817
---	---


APO AP 96343-5010 FY20 MCA PN77833 VEHICLE MAINTENANCE SHOP	VMS - BUILDING SECTIONS (CLIN 0001)
--	-------------------------------------

SHEET ID VMS S-A303

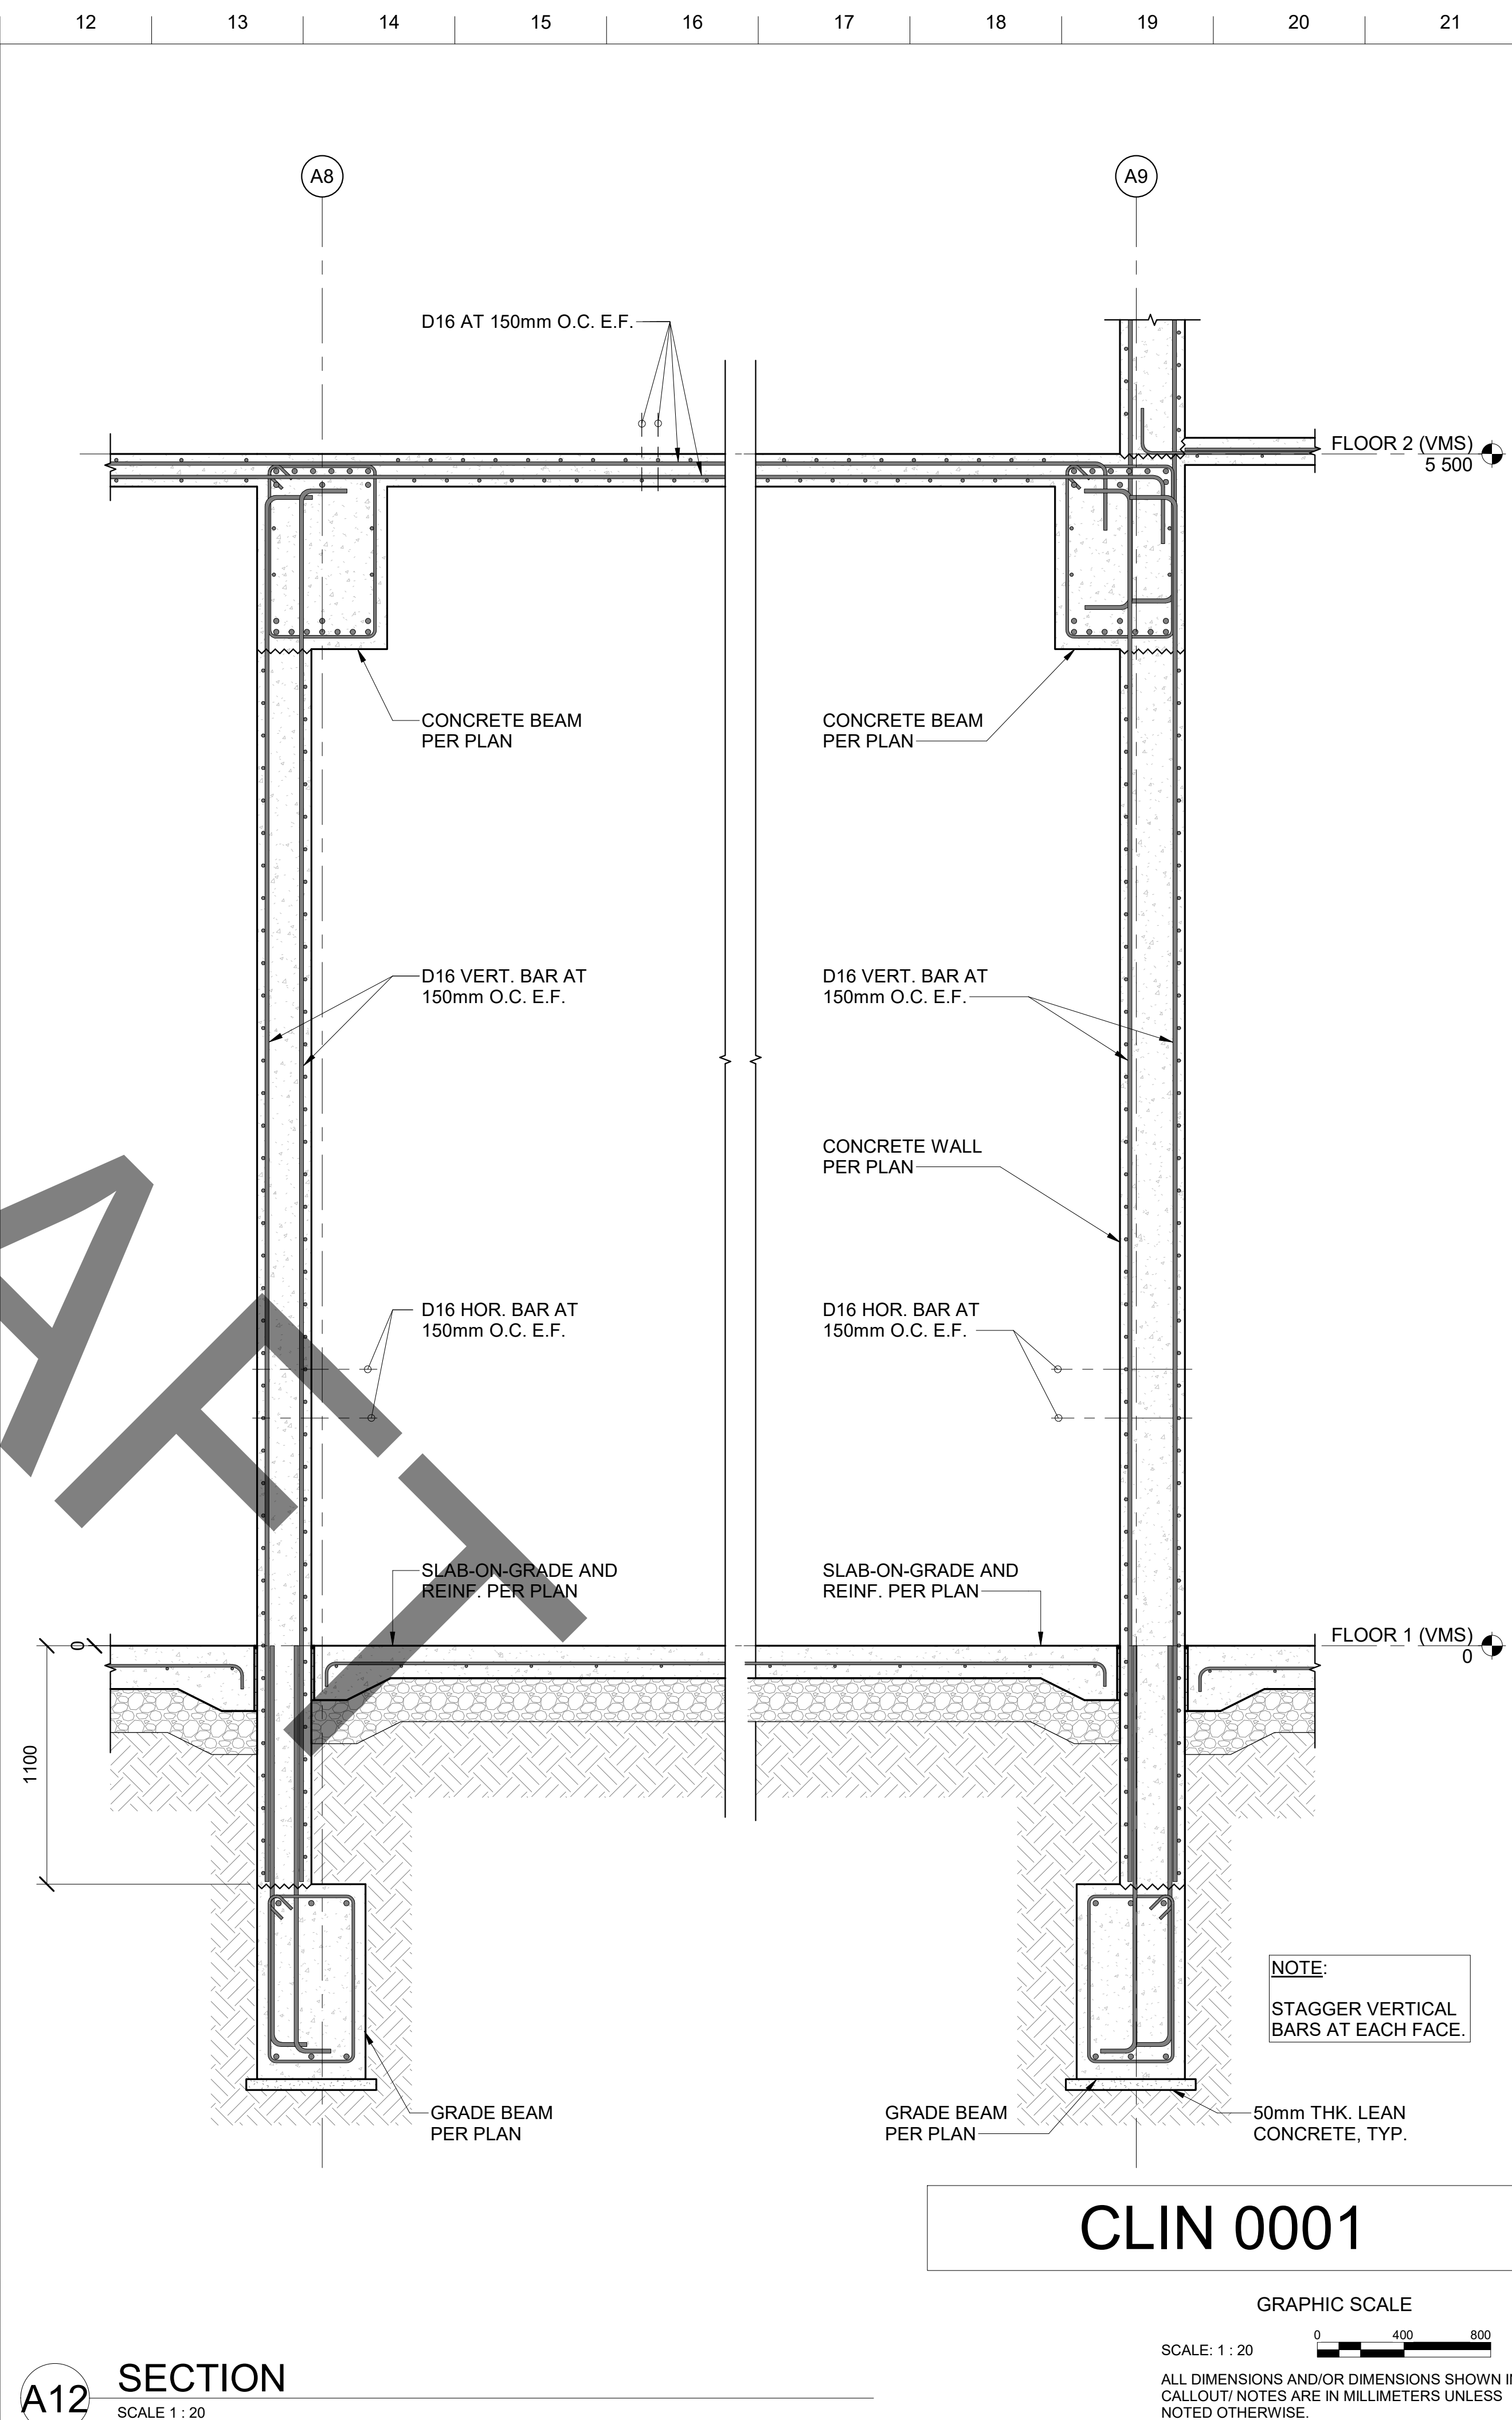

**U.S. Army Corps
Engineers®**

[illegible]

 U.S. ARMY CORPS OF ENGINEERS JAGT OKINAWA AREA OFFICE APO AP 96378-3132	 SSM INTERNATIONAL, INC. 500 KOWALEWICZ BLVD. #20 HONOLULU, HAWAII 96817	J. RABANAL DRAWN BY:	JUNE 2018 SOLICITATION NO.:
		J. UNO CHECKED BY:	W912HV-17-D-0003 CONTRACT NO.:
		J. UNO SUBMITTED BY:	
		J. UNO ANSID	

PT20 IACA FN/7833 VEHICLE MAINTENANCE SHOP


SHEET ID
VMS
A502

Autodesk Docs://Vehicle Maint Shop Kadena/511758_TEMF_STRUC.M

File Path:

Plot Date: 12/16/2025 3:36:04 PM

INTERMEDIATE DESIGN

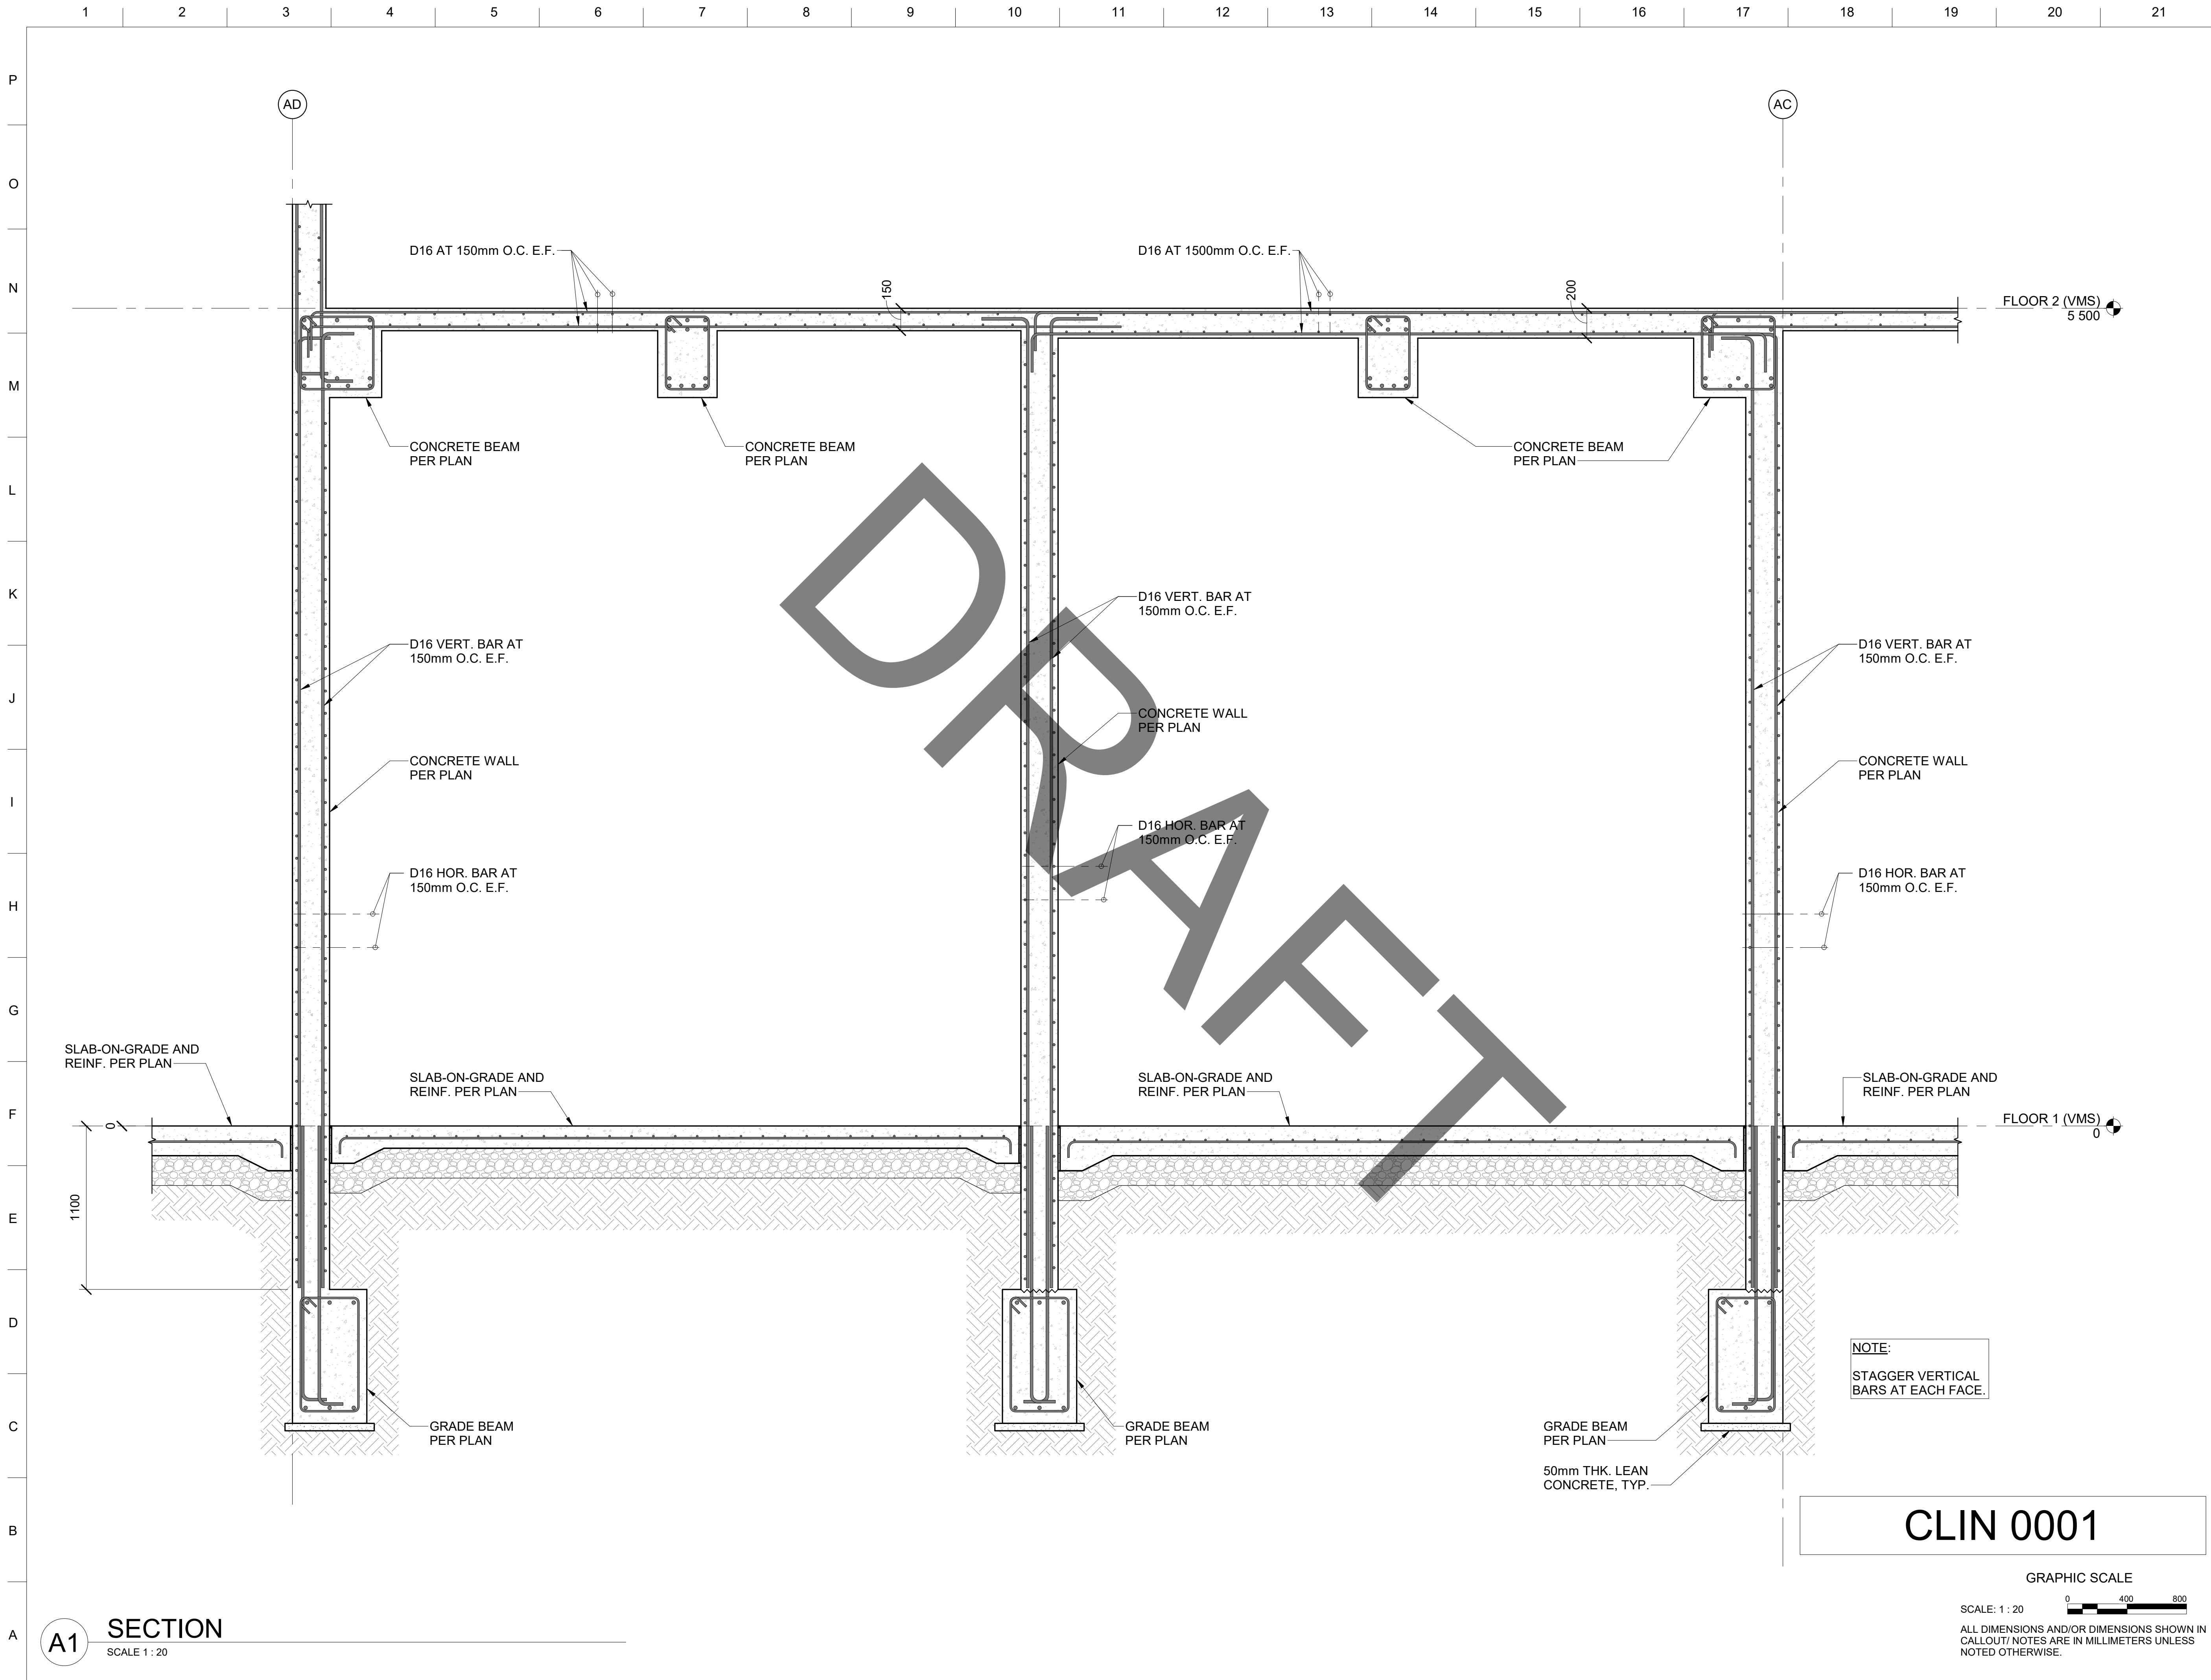

US Army Corps of Engineers®

ISSUE DATE:		SOLICITATION NO.:		CONTRACT NO.:		MARK		DATE	
JUNE 2018				W9124V-17-D-0003					
DESIGNED BY:		DRAWN BY:		CHECKED BY:		SUBMITTED BY:		ANSI D	
J. RABANAL		R. TANGONAN		J. JUNO					

US ARMY CORPS OF ENGINEERS
JAPAN ENGINEER DISTRICT
OKINAWA AREA OFFICE
APO AP 96376-5132

SSFM
SSFM INTERNATIONAL INC.
507 SUMNER STREET, SUITE 620
HONOLULU, HAWAII 96817




APO AP 96343-5010
FY20 MCA PN77833 VEHICLE MAINTENANCE SHOP


VMS - SECTIONS AND DETAILS (CLIN 0001)



SHEET ID
VMS
S-A503

Plot Date: 12/16/2025 3:36:05 PM
File Path: Autodesk Docs / Vehicle Maint Shop / Kadena511756 / TEMP / STRUCT.dwg

INTERMEDIATE DESIGN

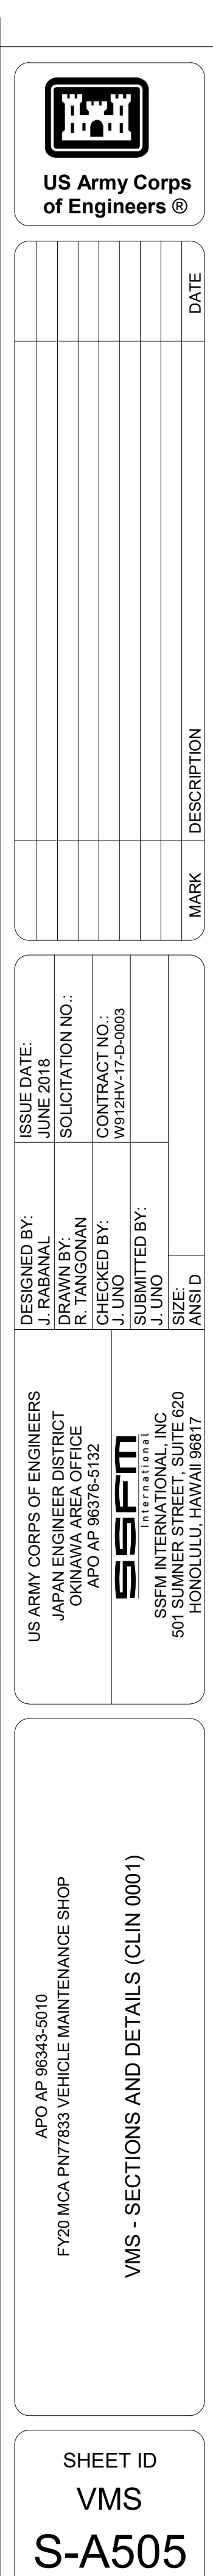 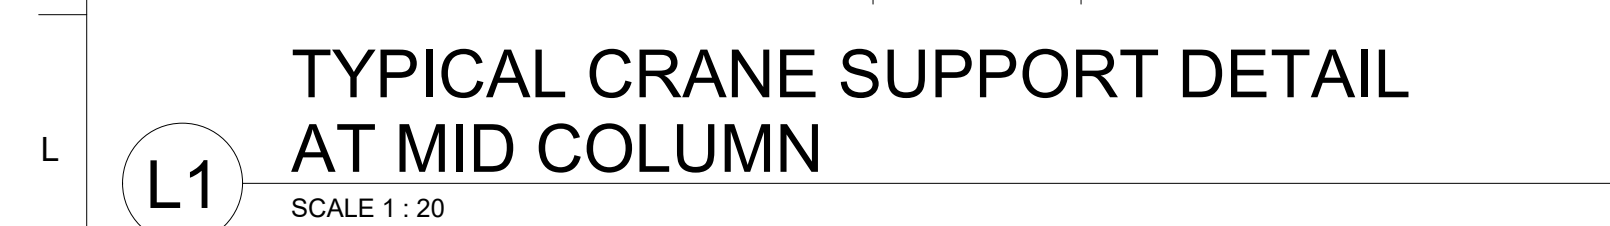

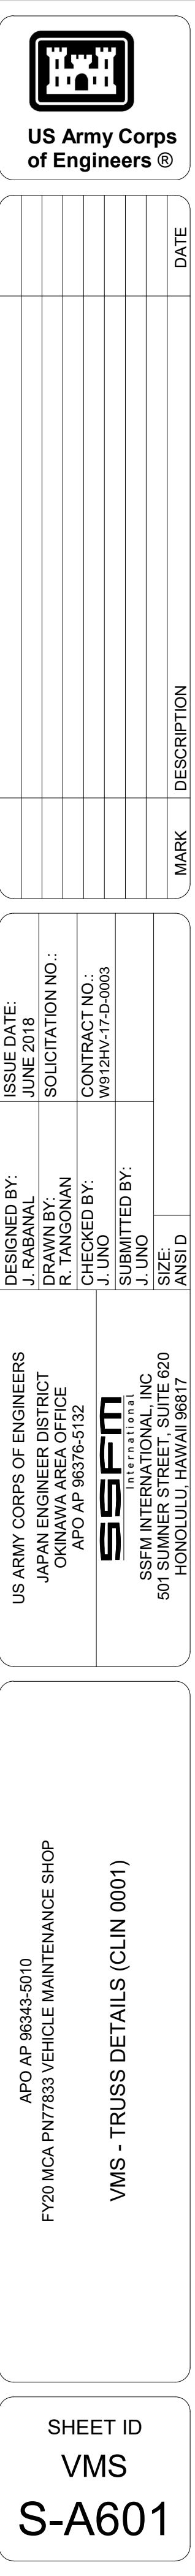

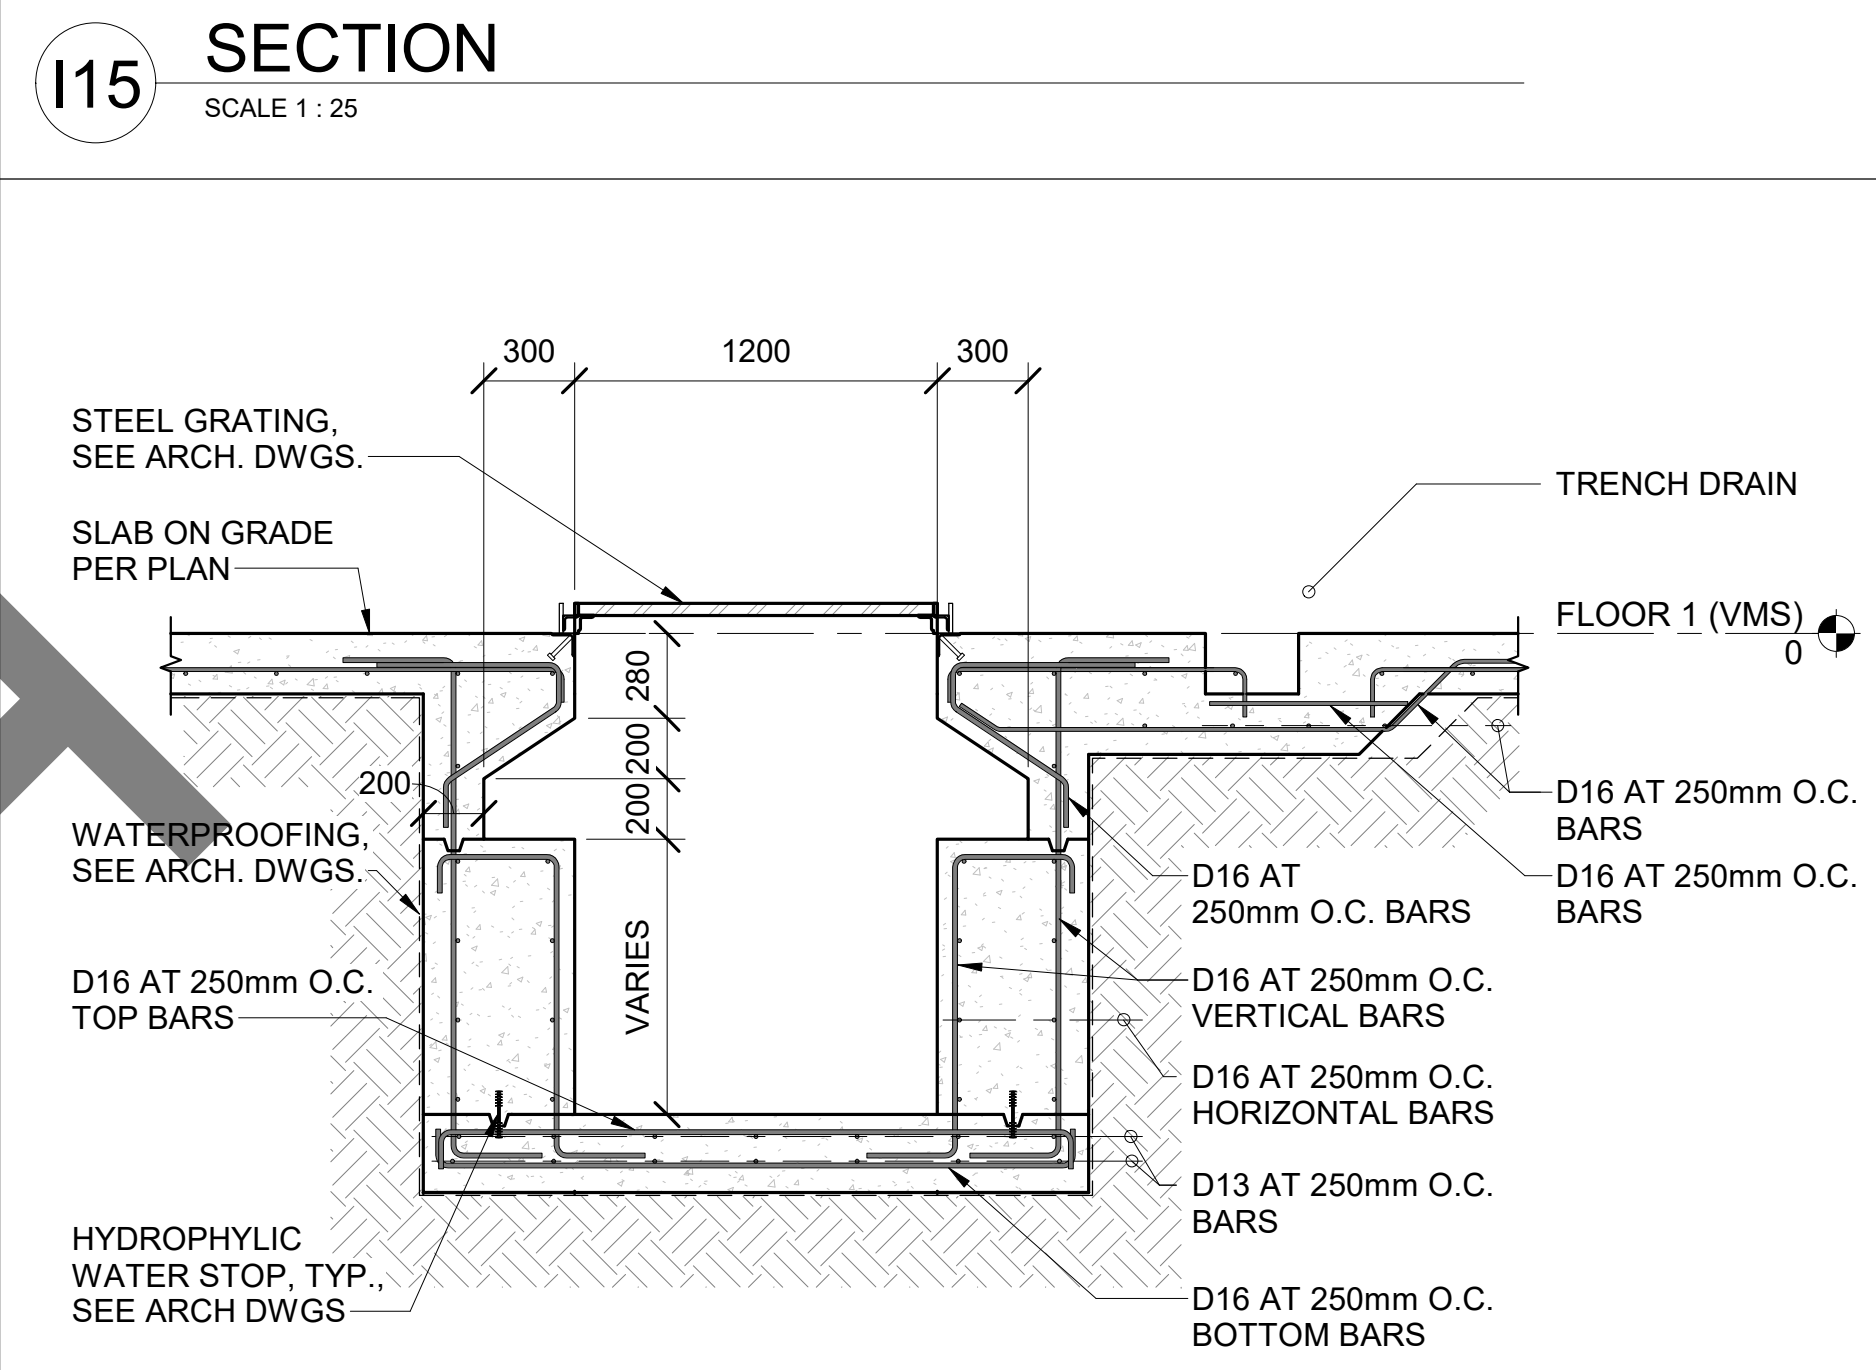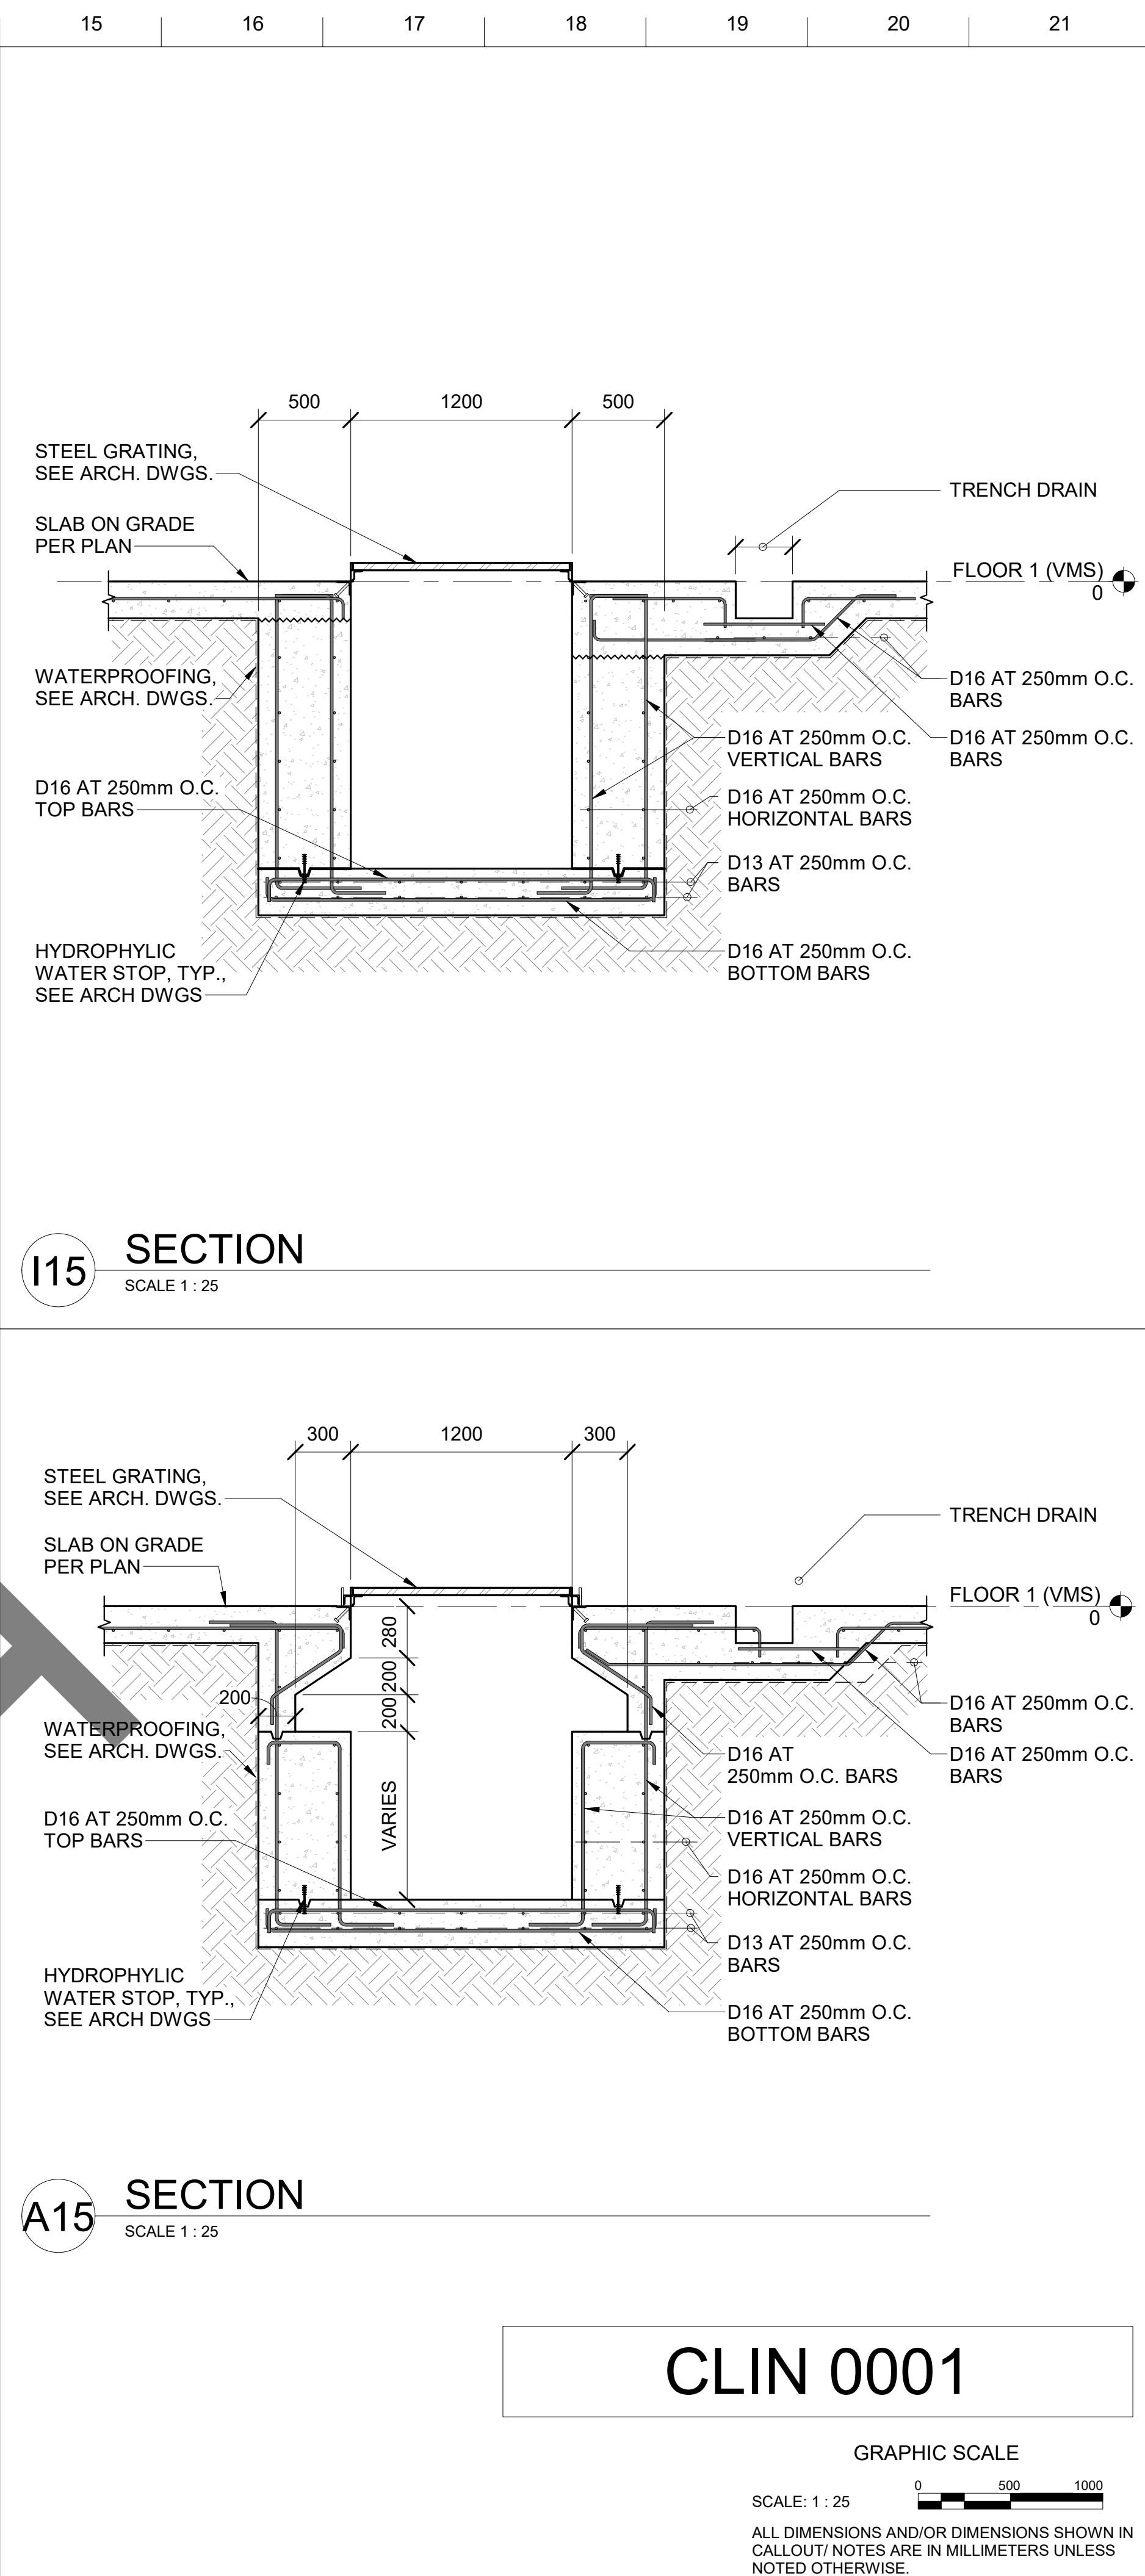


A15 SECTION
SCALE 1 : 25


GRAPHIC SCALE

SCALE: 1 : 25



ALL DIMENSIONS AND/OR DIMENSIONS SHOWN IN
CALLOUT/NOTES ARE IN MILLIMETERS UNLESS
NOTED OTHERWISE.

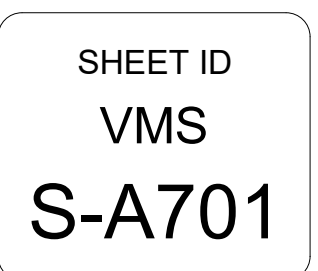

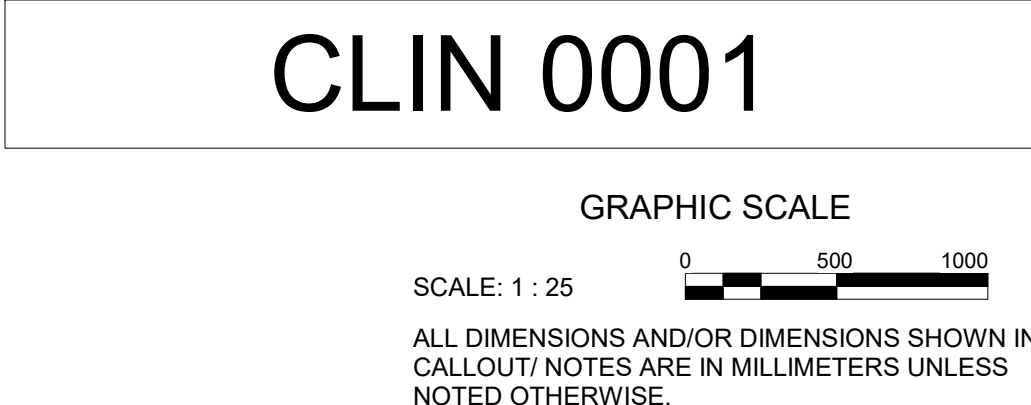

INTERMEDIATE DESIGN

[illegible]

US ARMY CORPS OF ENGINEERS JAPAN DISTRICT OKINAWA AREA OFFICE APO AP 96376-5132		JUNE 2018 J. RABANAL DRAWN BY CHECKED BY: J. UNO SUBMITTED BY: J. UNO ANSI D		SOLICITATION NO.: CONTRACT NO.: W912HJV-17-D-0003
--	--	---	--	---

VMS - ELEVATOR FOUNDATION, FRAMING PLAN
AND SECTION (CLIN 0001)

SHEET ID
VMS
-A703

Autodesk Docs://Vehicle Maint Shop Kadana/511758_TEMF_STRUC.MI

Plot Date: 12/16/2025 3:46:55 PM

INTERMEDIATE DESIGN




GRAPHIC SCALE

SCALE: 1 : 25


0 500 1000

ALL DIMENSIONS AND/OR DIMENSIONS SHOWN WITH
CALLOUT/ NOTES ARE IN MILLIMETERS UNLESS
NOTED OTHERWISE.



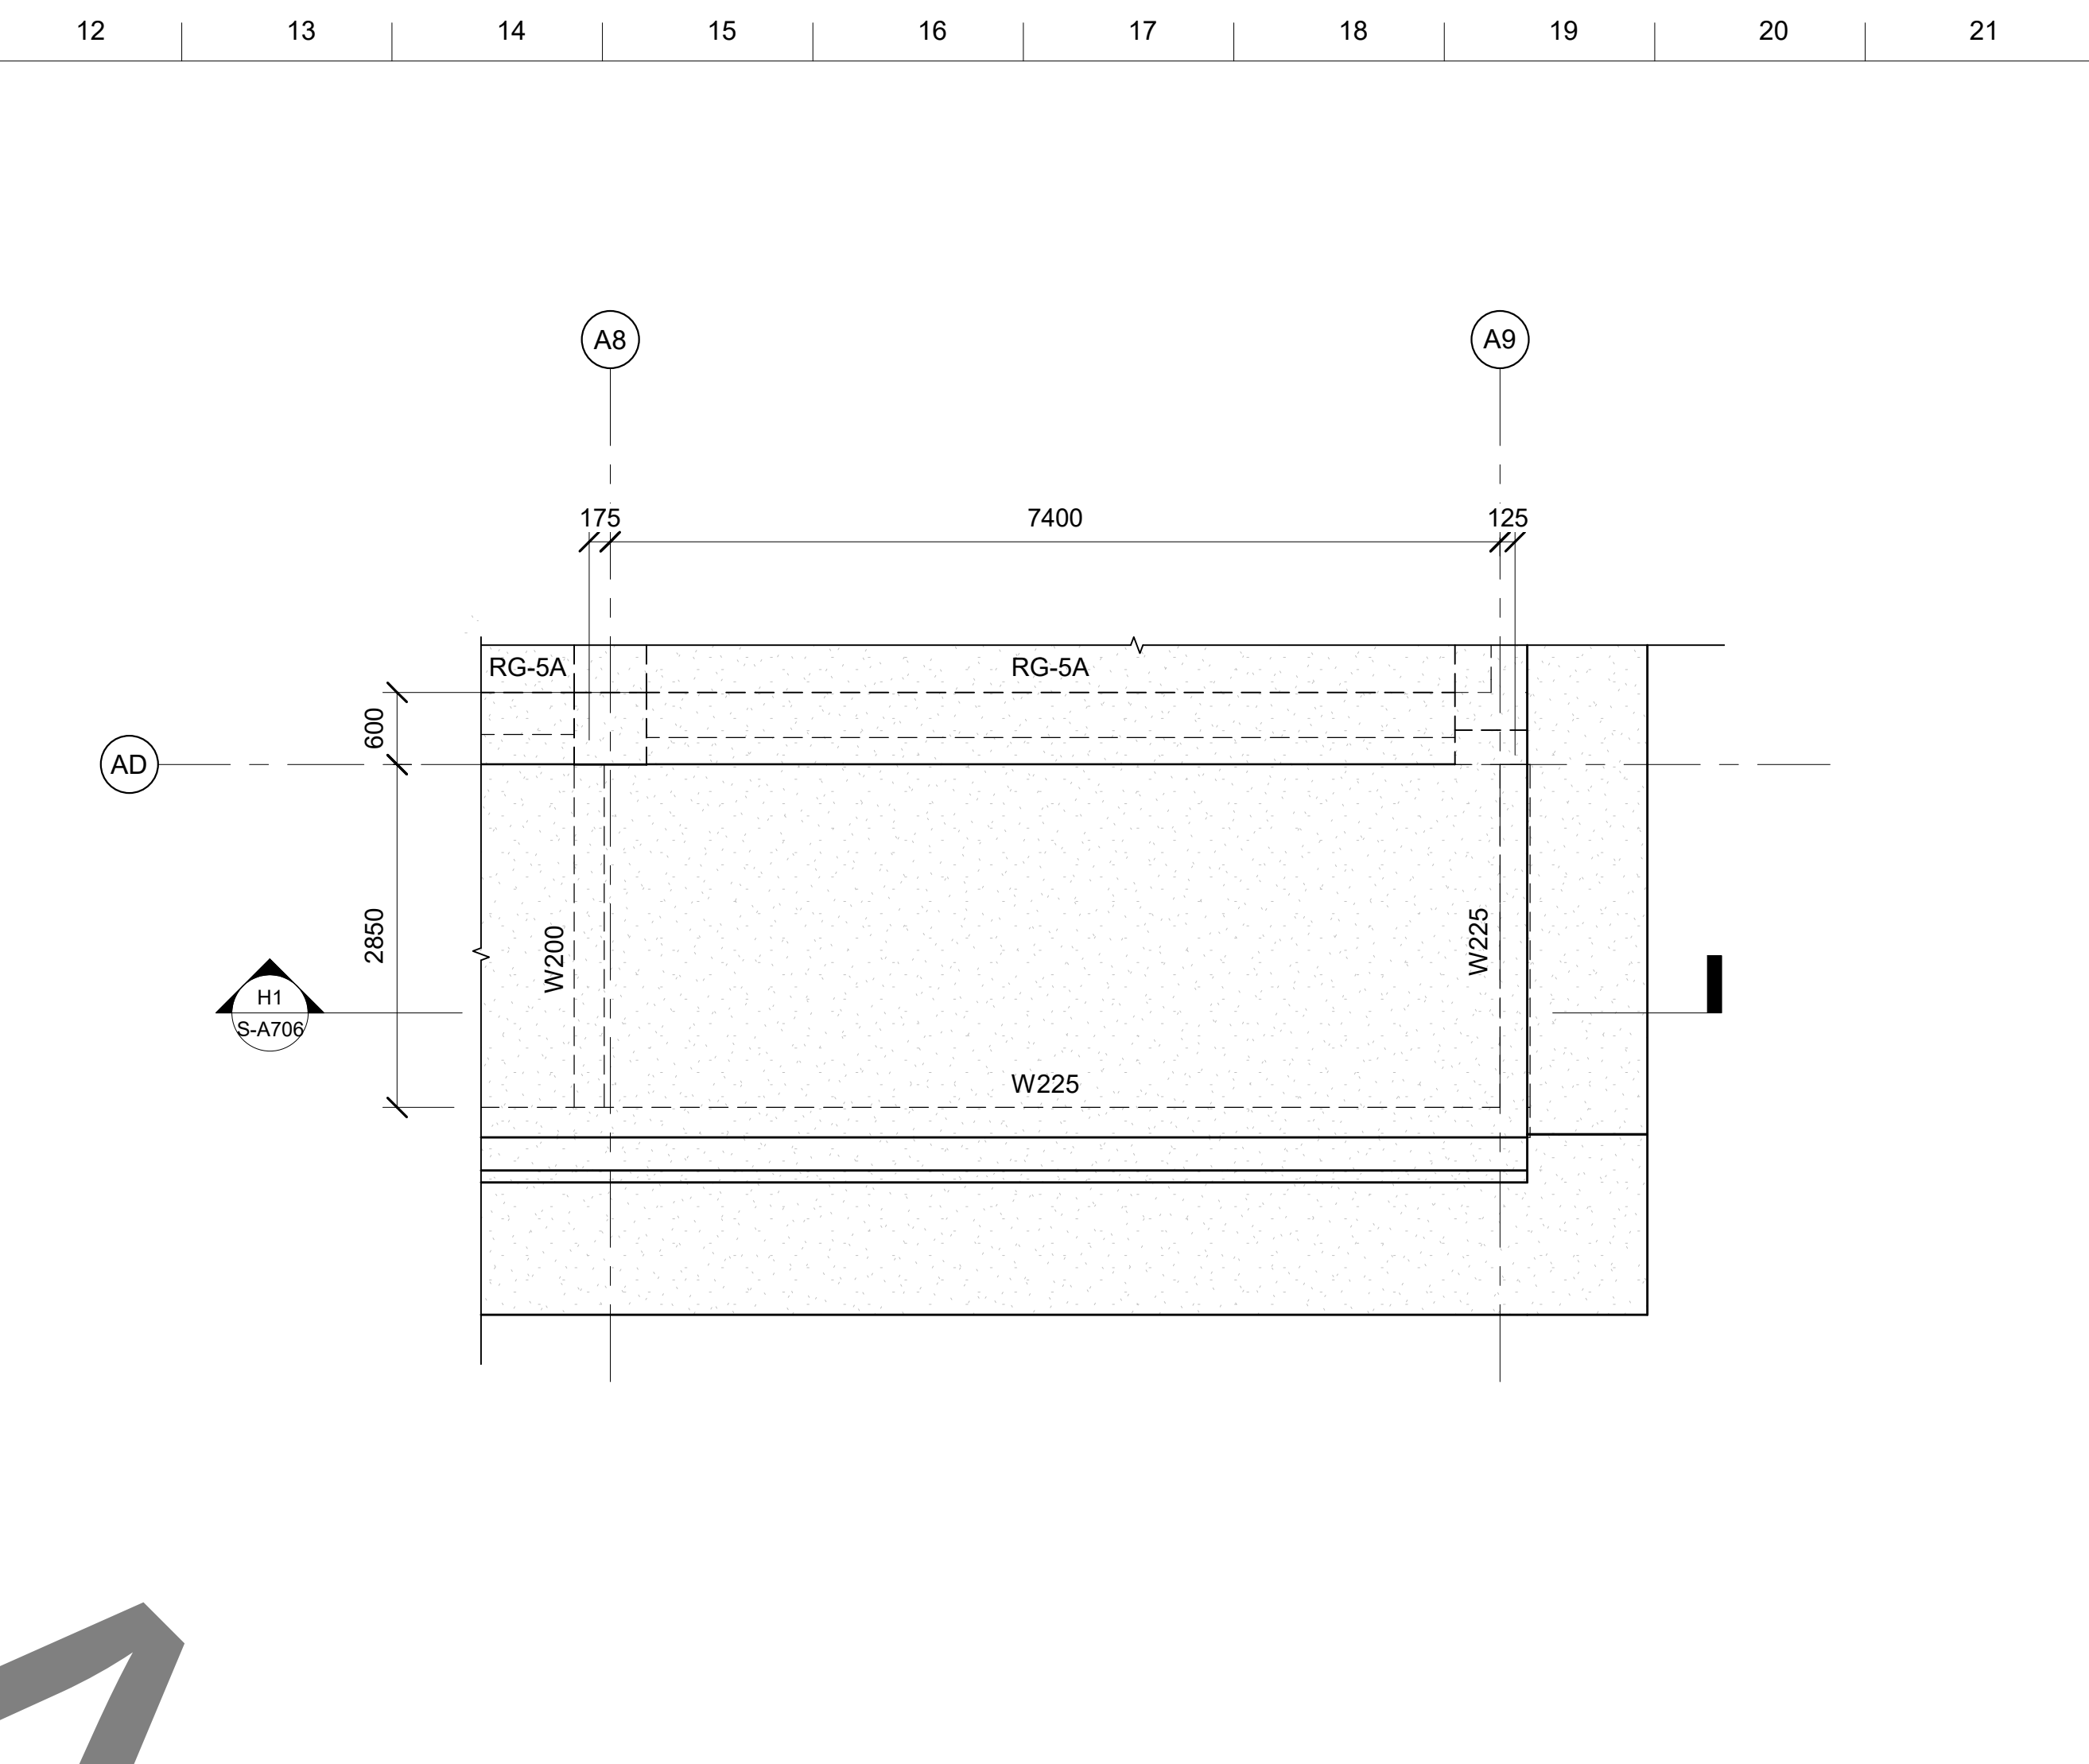


H12 VMS - STAIR 2 ROOF FRAMING PLAN PLAN (CLIN 0001)
SCALE 1 : 50

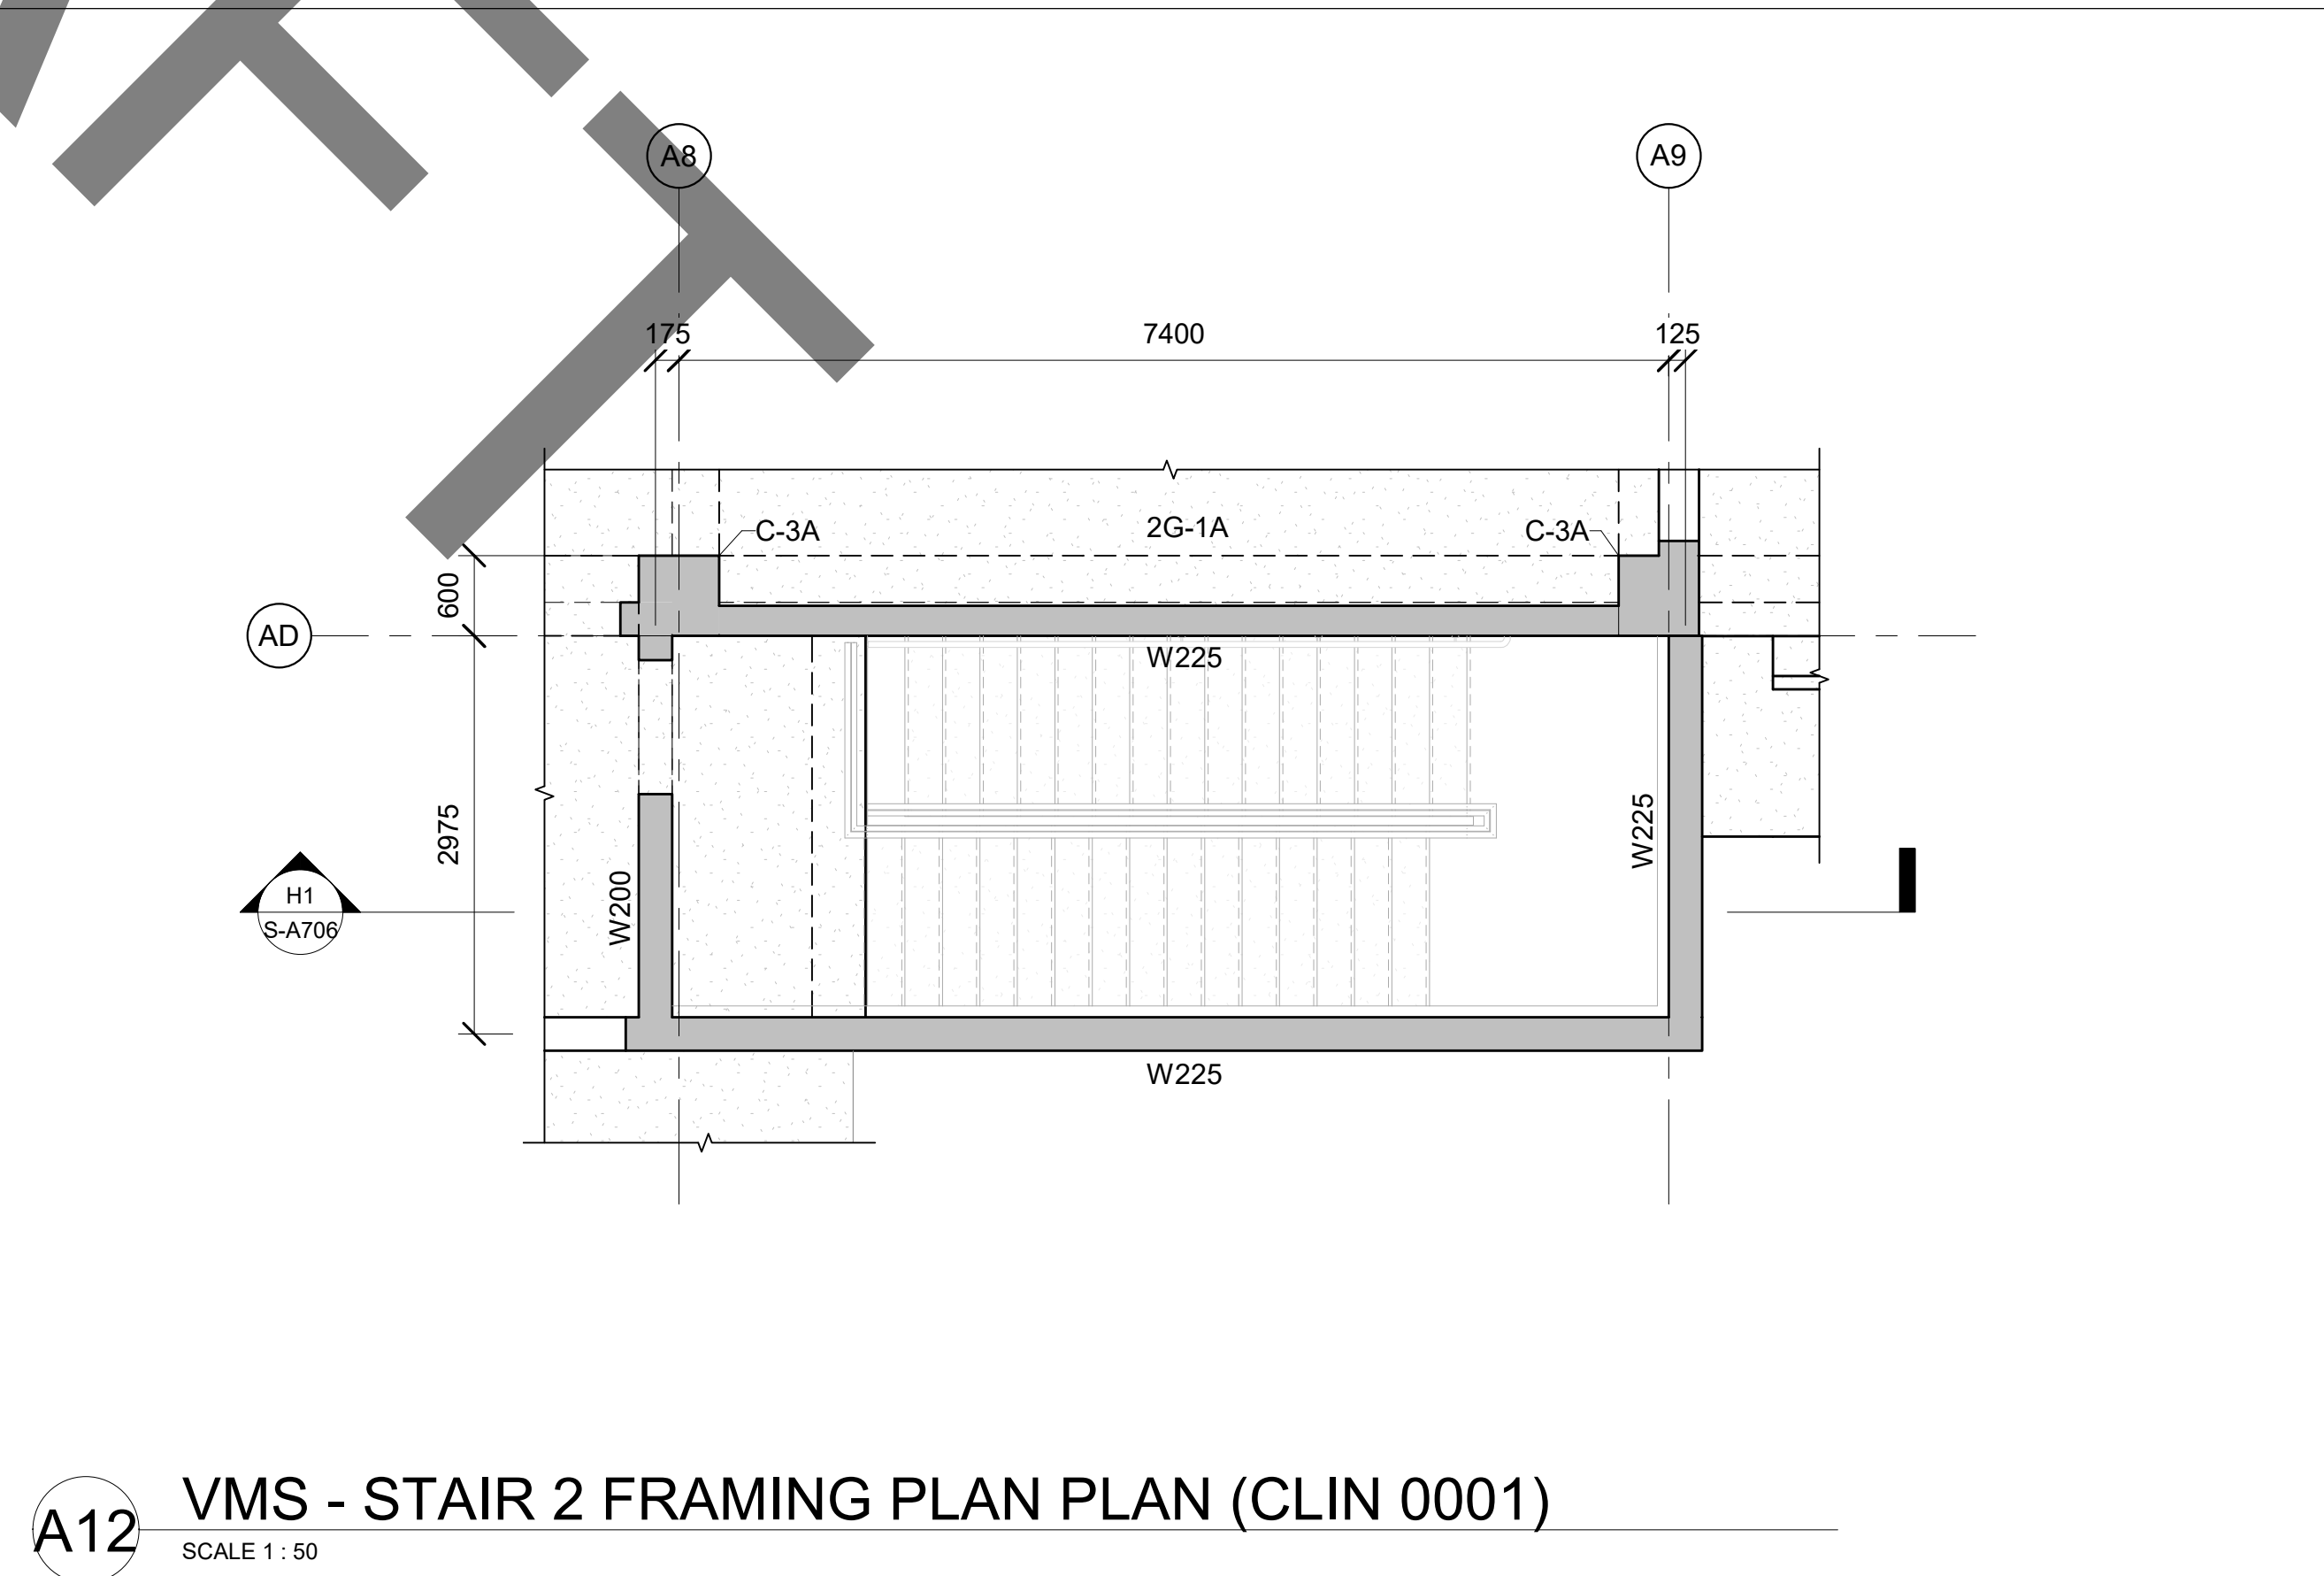

A12 VMS - STAIR 2 FRAMING PLAN PLAN (CLIN 0001)
SCALE 1 : 50



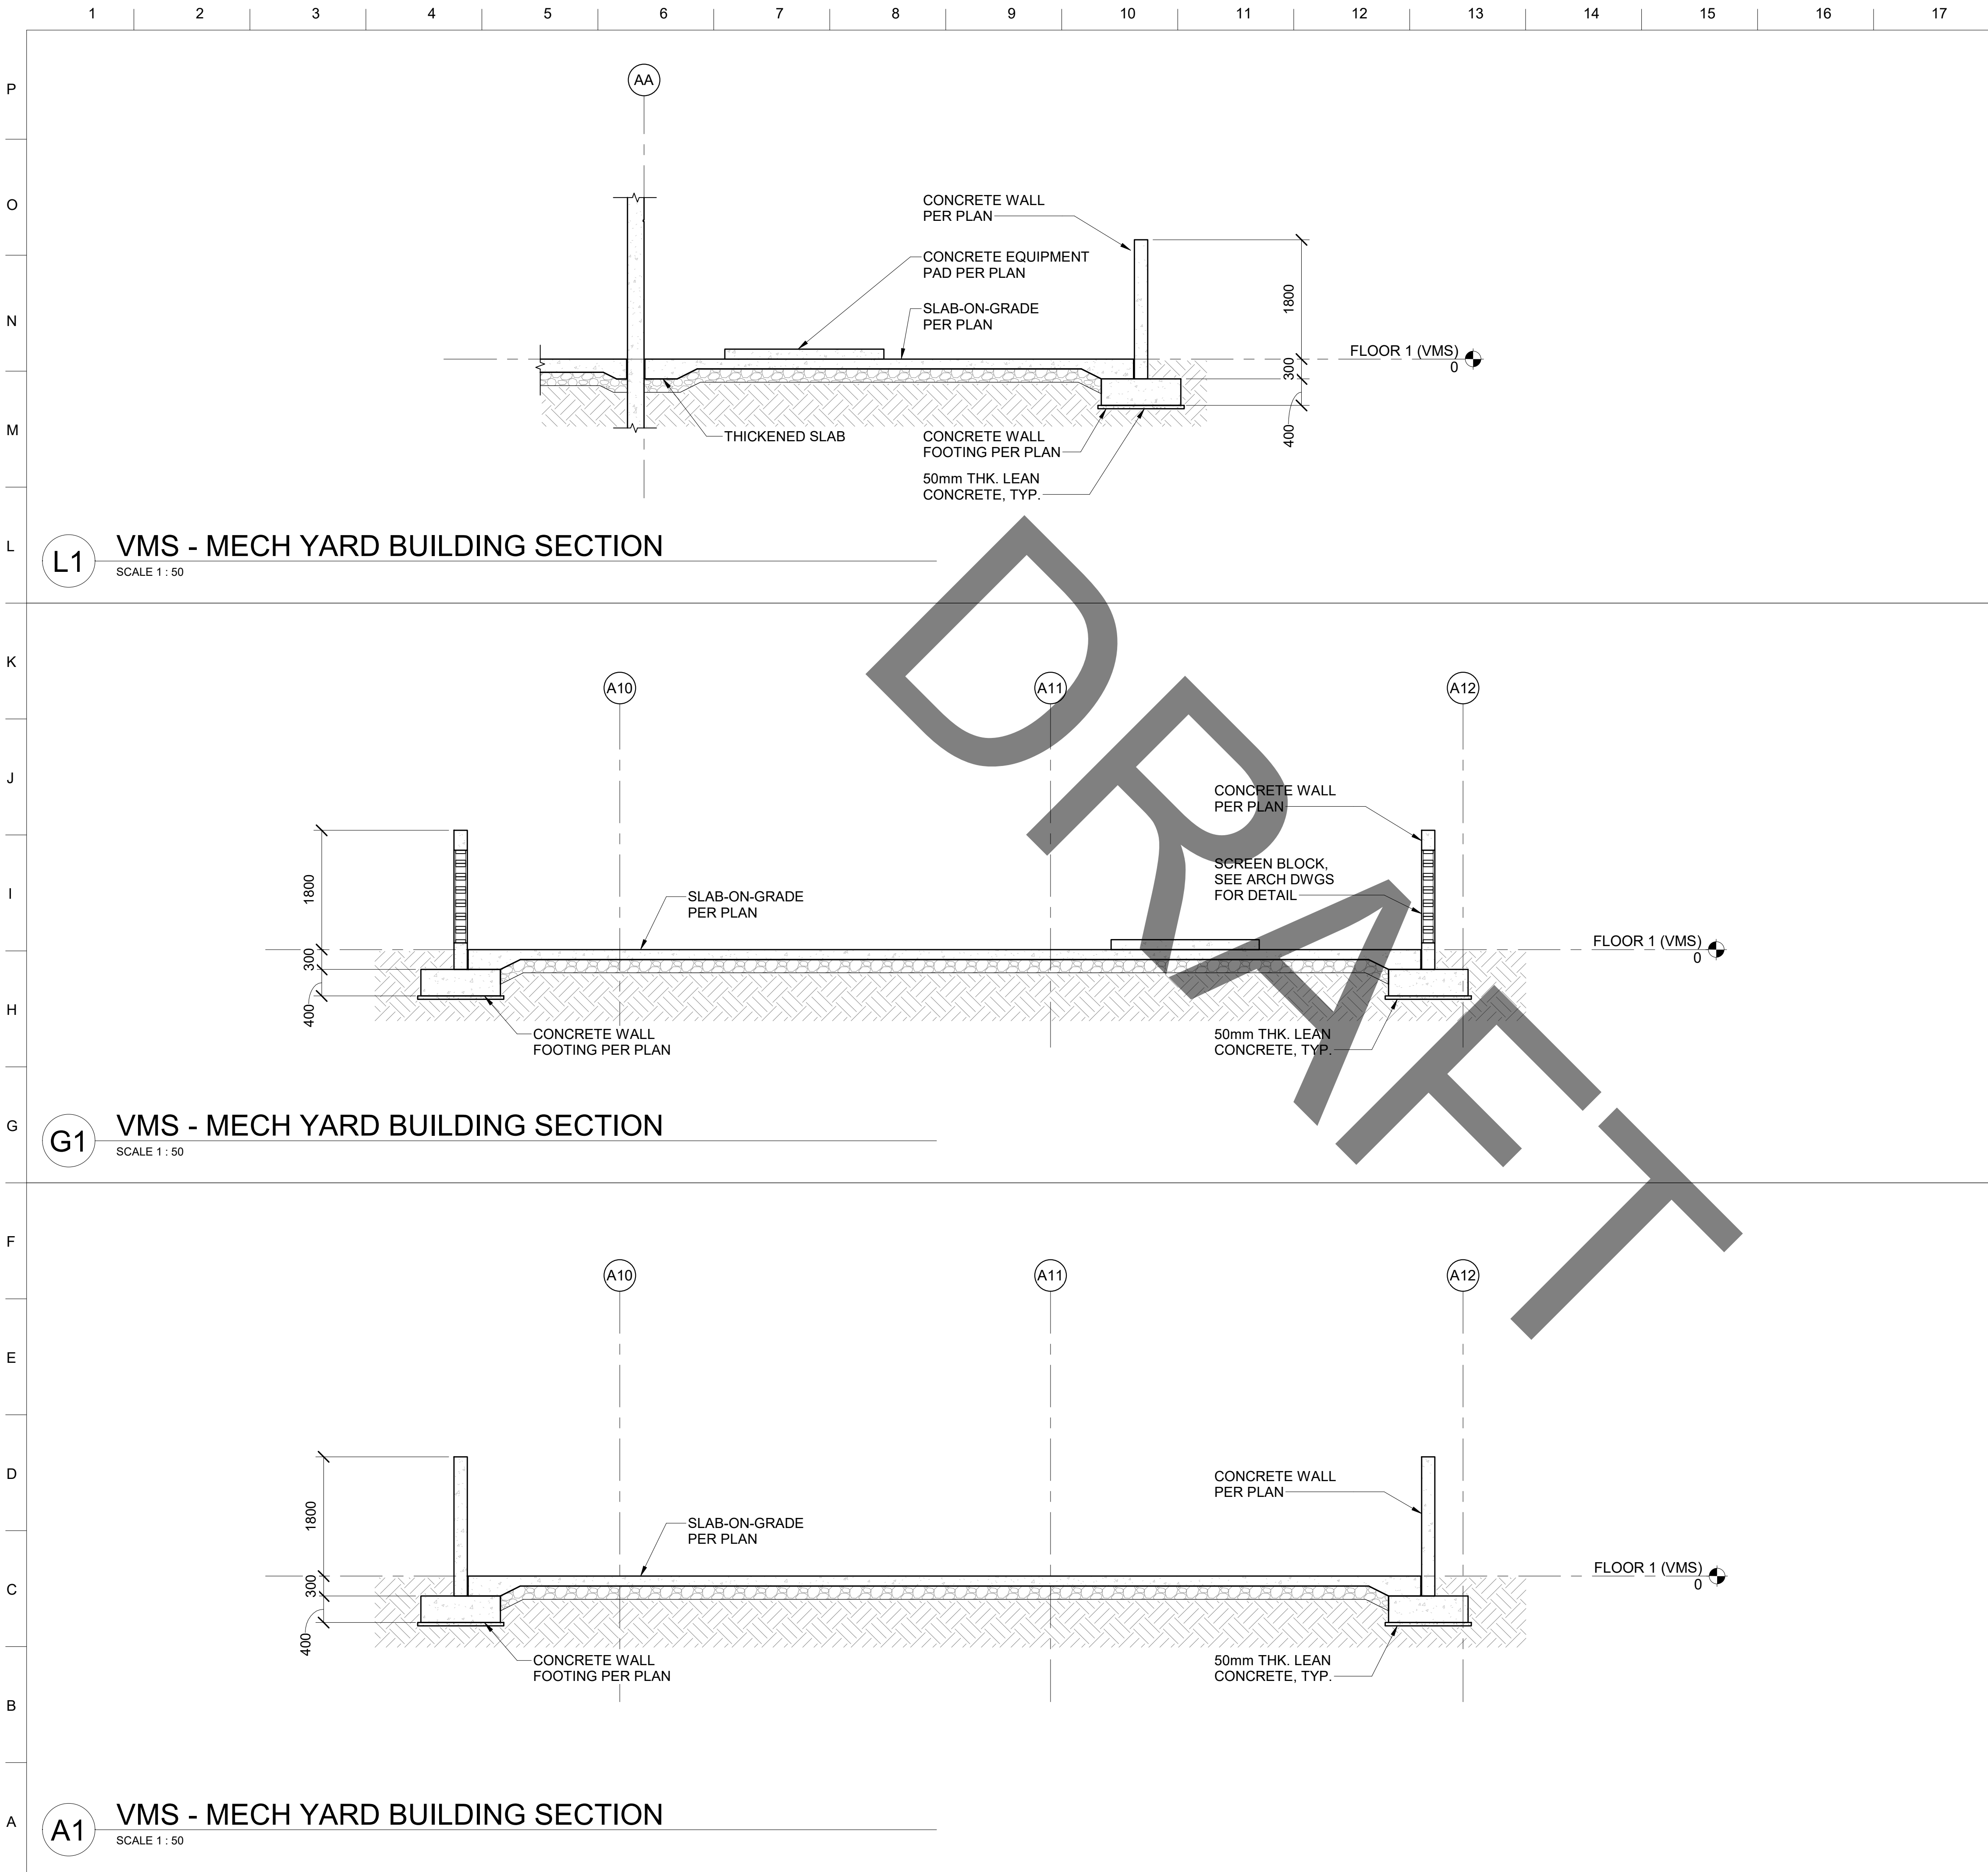

REFERENCE DRAWINGS

S-001 - GENERAL NOTES
S-002 - DESIGN DATA, DESIGN CODES AND STANDARDS, ABBREVIATION
S-501 - TYPICAL REINFORCING STEEL DETAILS
S-502 - TYPICAL CONCRETE DETAILS
S-604 - CONCRETE FOOTING SCHEDULE
S-605 - CONCRETE WALL SCHEDULE

NOTES

1. SEE ARCHITECTURAL DRAWINGS FOR DIMENSIONS, ELEVATIONS AND DETAILS NOT SHOWN ON STRUCTURAL DRAWINGS.

2. SEE ARCHITECTURAL DRAWINGS FOR FLOOR SLOPE.

3. VERIFY WITH ARCHITECT/MECHANICAL FOR SIZE AND LOCATION OF OPENINGS.

CLIN 0001

GRAPHIC SCALE

GRAPHIC SCALE

SCALE: 1 : 50

0 1000 2000

ALL DIMENSIONS AND/OR DIMENSIONS SHOWN IN CALLOUT/ NOTES ARE IN MILLIMETERS UNLESS NOTED OTHERWISE.

US Army Corps of Engineers®

ISSUE DATE:
JUNE 2018

DESIGNED BY:
J. RABANAL

US ARMY CORPS OF ENGINEERS
JAPAN ENGINEER DISTRICT
OKINAWA AREA OFFICE
APO AP 96376-5132

SSFM

STRUCTURAL STEEL FABRICATION METHOD

SSFM INTERNATIONAL, INC.
507 SUMNER STREET, SUITE 620
HONOLULU, HAWAII 96817

CONTRACT NO.:
W72HWY-17-D-0003

CHECKED BY:
J. UNO

SIZE:
ANSI D

DATE

DESCRIPTION

MARK

CLIN 0001

AP O AP 96343-5010
FY20 MCA PN77833 VEHICLE MAINTENANCE SHOP

VMS - MECHANICAL YARD BUILDING SECTIONS (CLIN 0001)



SHEET ID

WT

S-A708

INTERMEDIATE DESIGN

Plot Date: 12/16/2025 3:36:37 PM File Path: AutoCAD Docs/Vehicle Maint Shop/Kadena517756_TEME_STRUCT.rvt

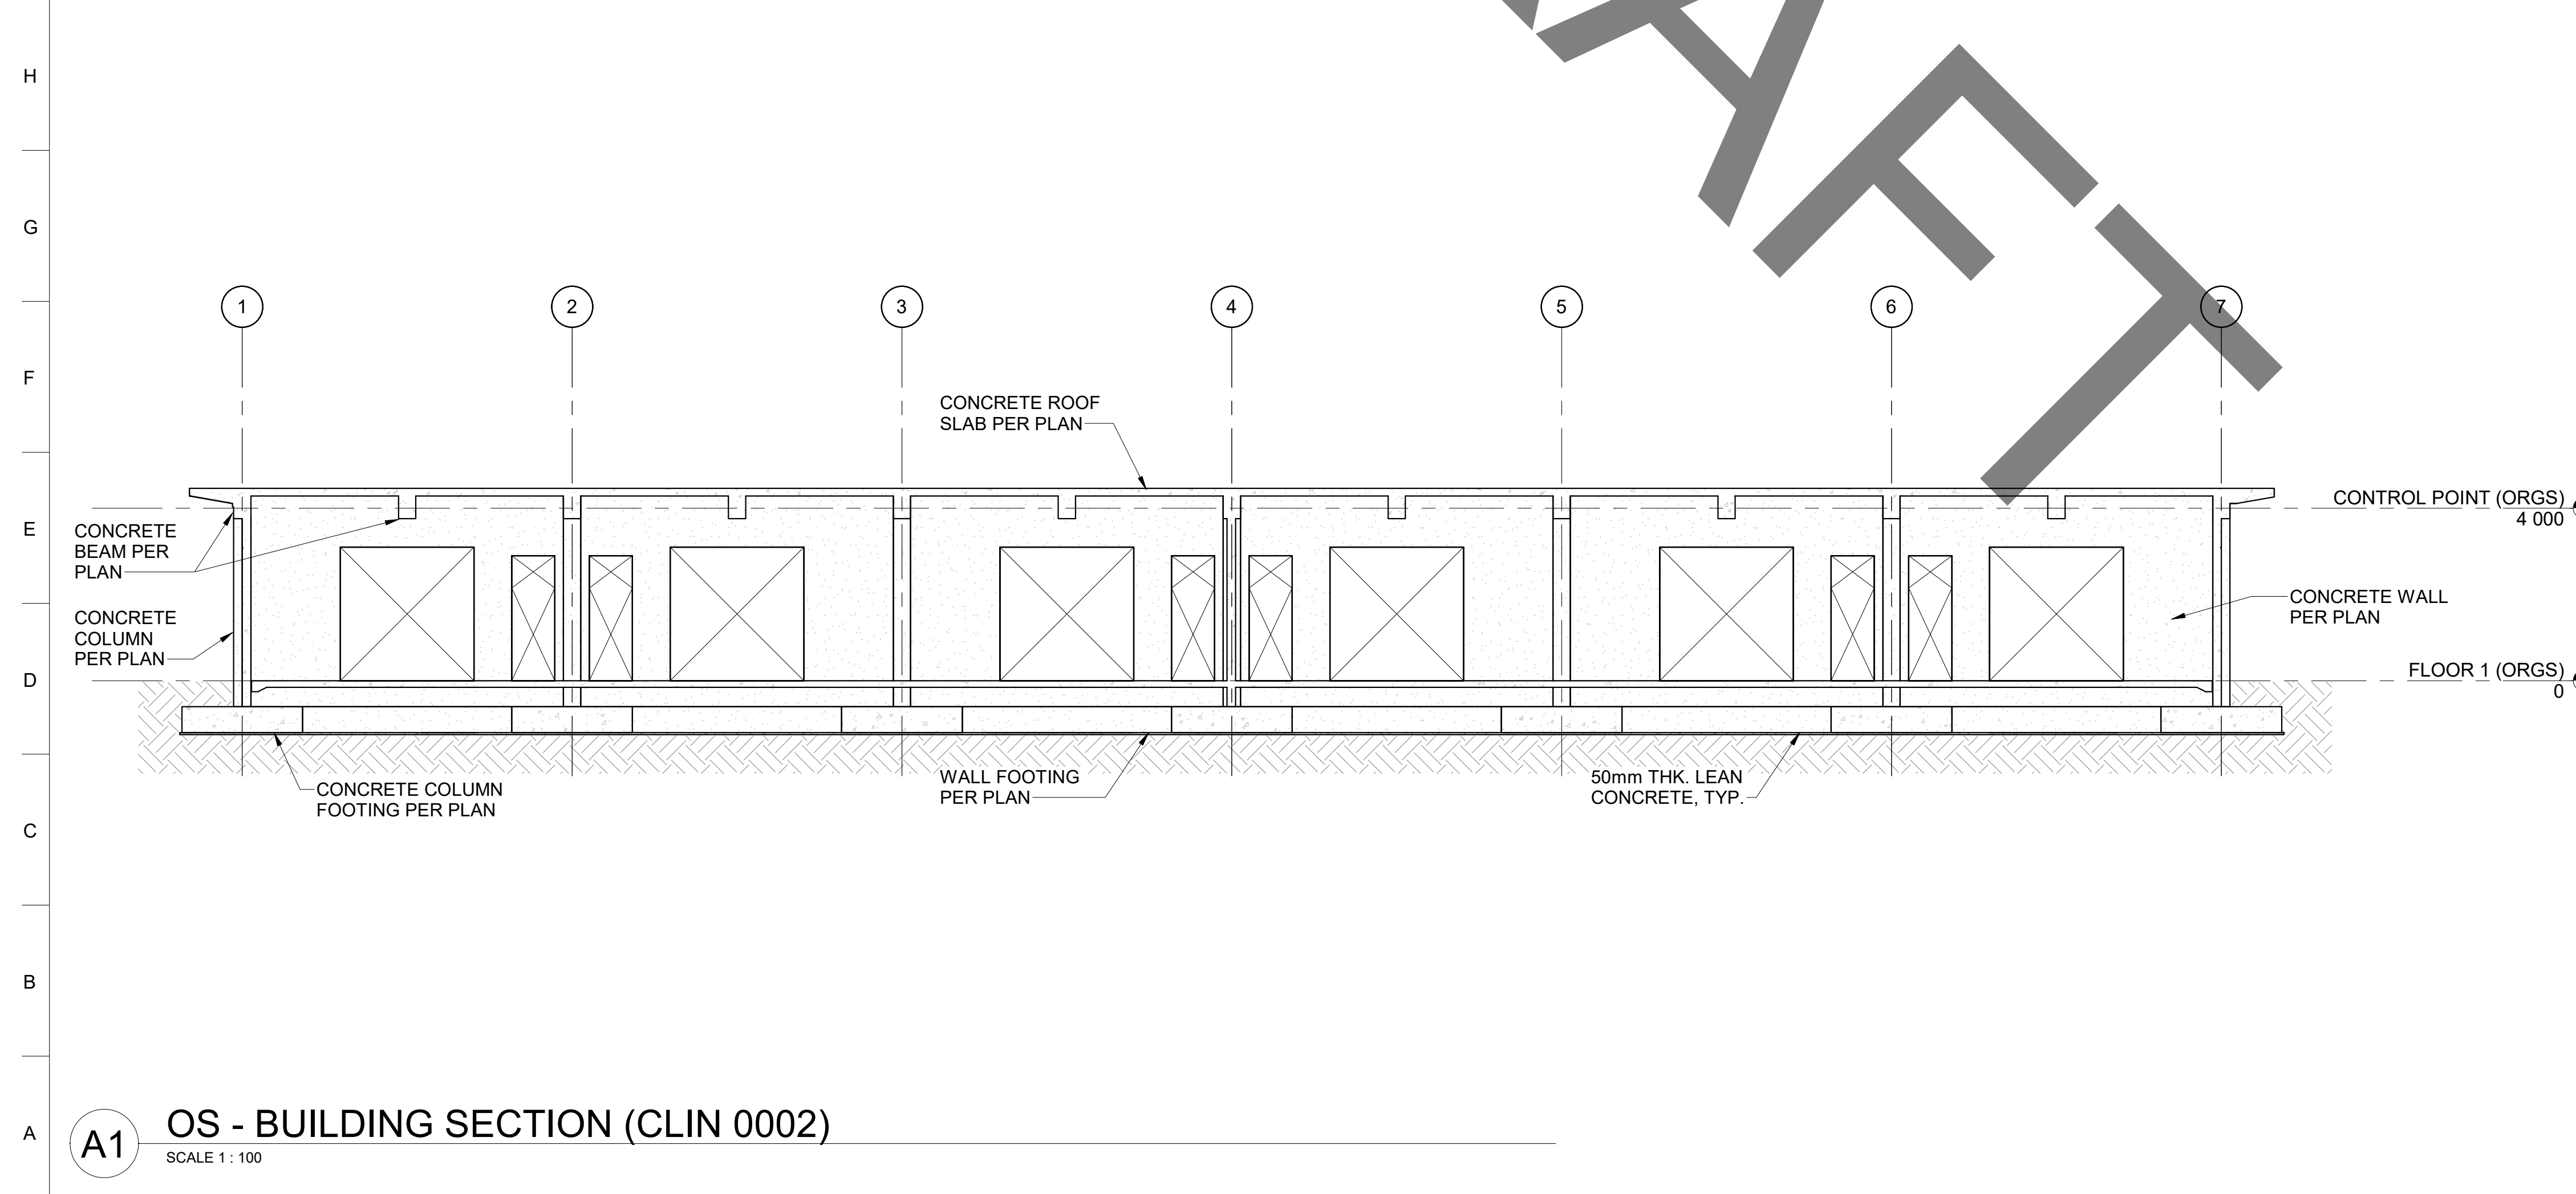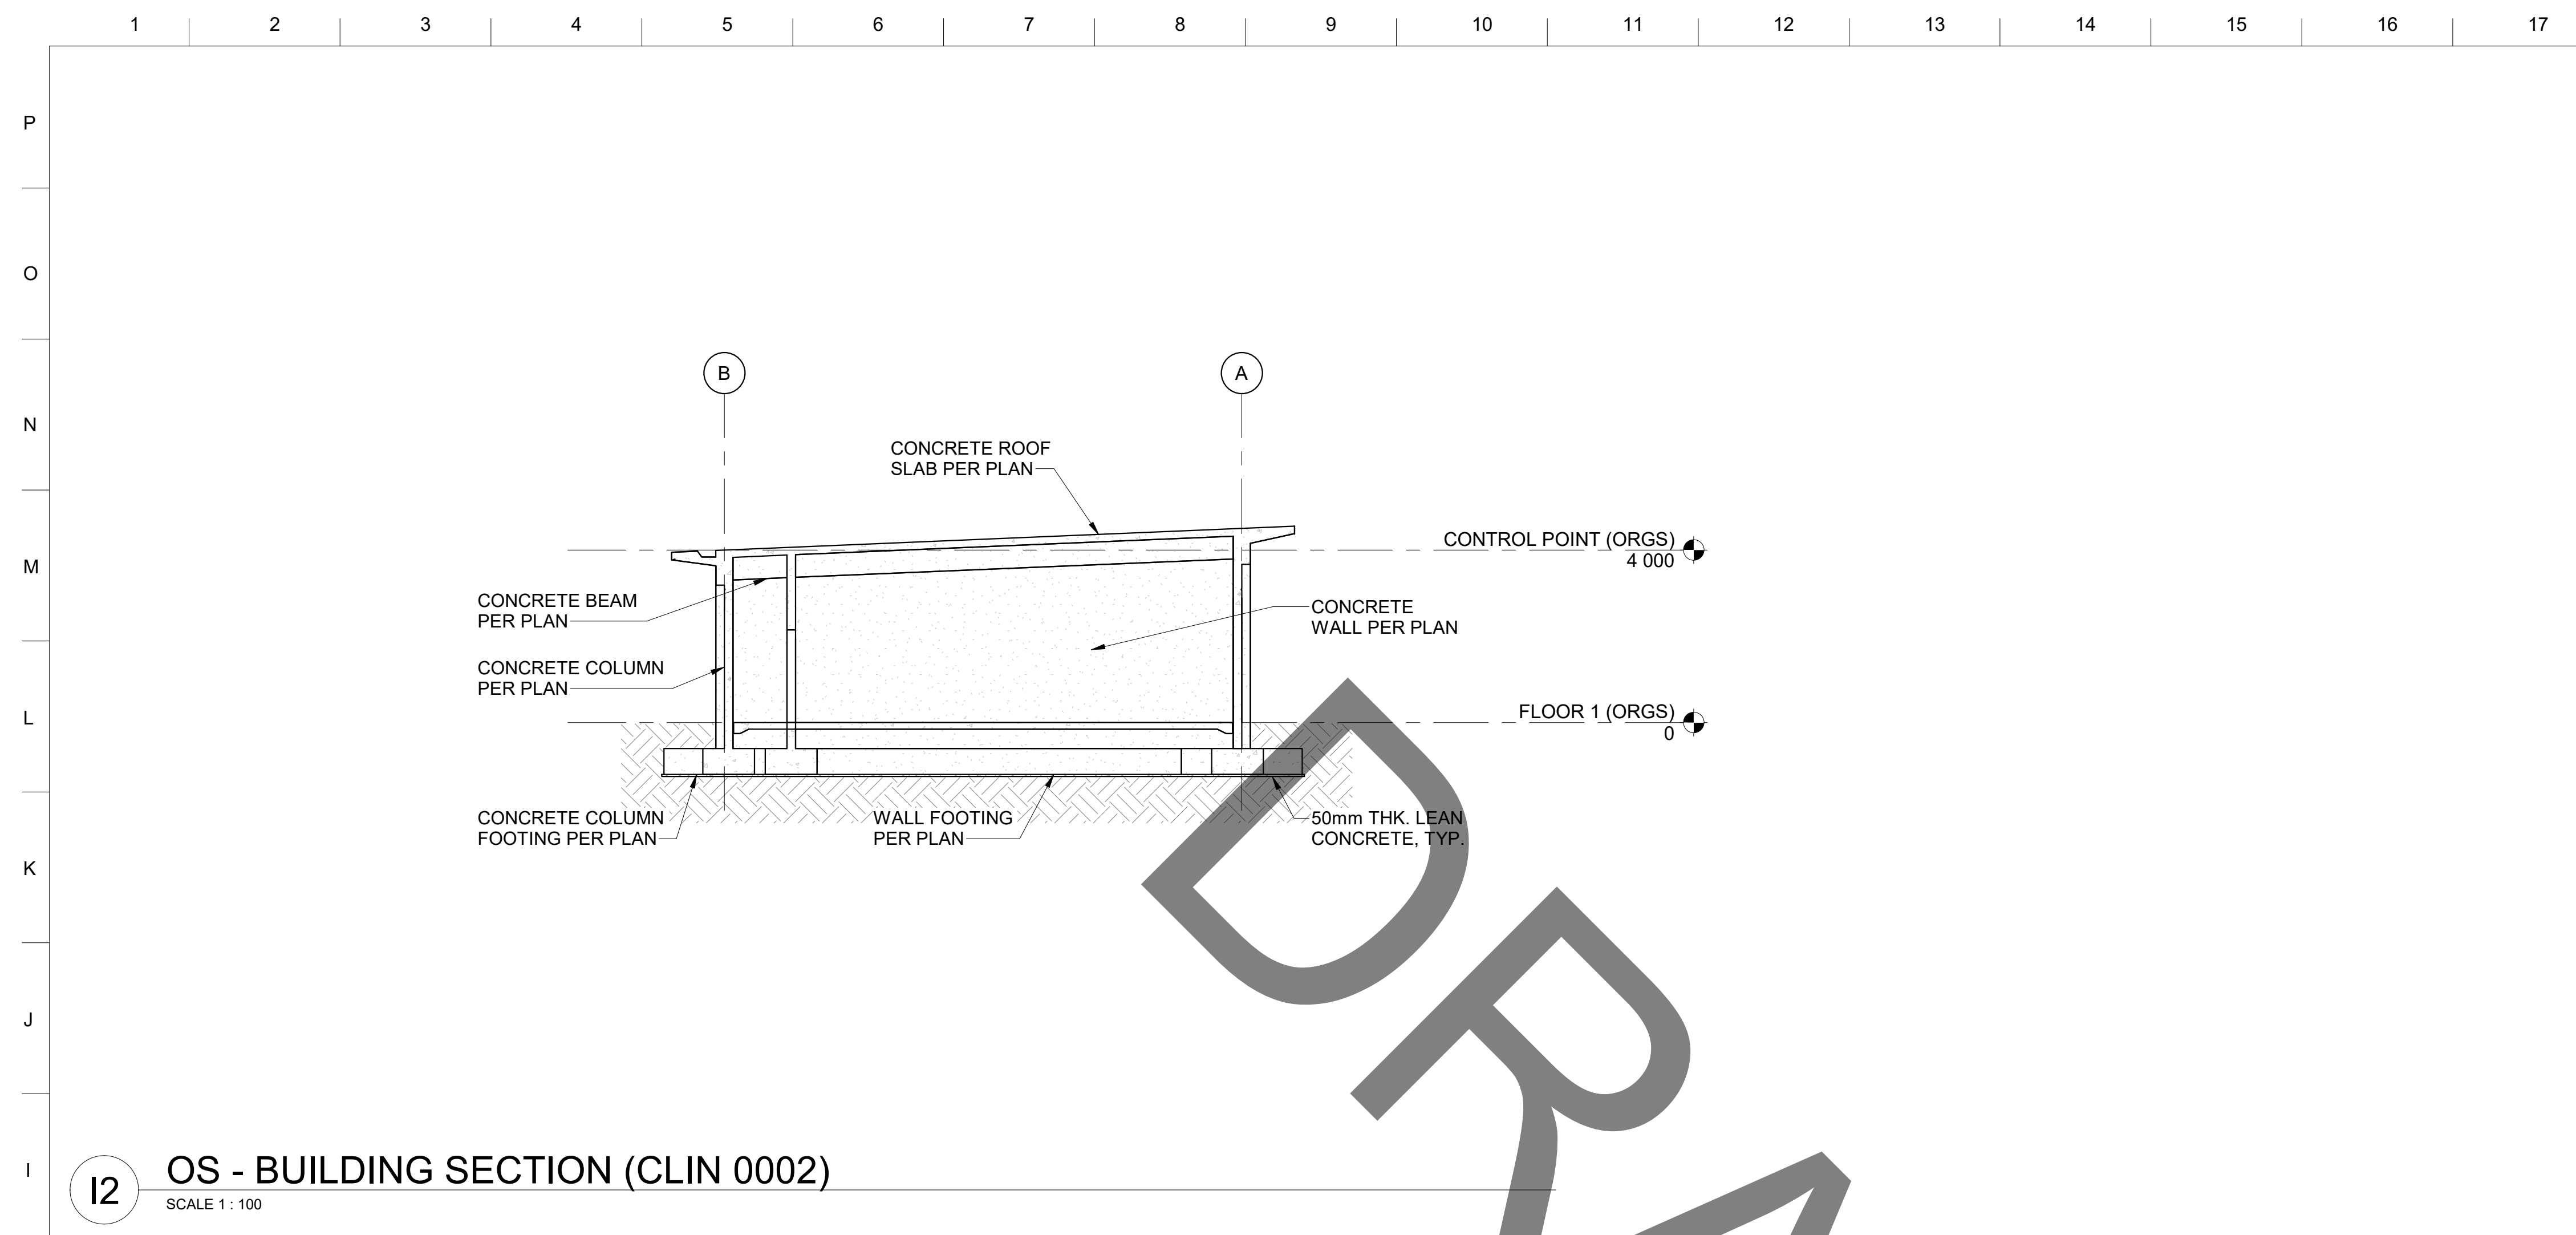

REFERENCE DRAWINGS

S-001 - GENERAL NOTES
S-002 - DESIGN DATA, DESIGN CODES AND STANDARDS,
ABBREVIATION
S-501 - TYPICAL REINFORCING STEEL DETAILS
S-502 - TYPICAL CONCRETE DETAILS
S-604 - CONCRETE FOOTING SCHEDULE
S-605 - CONCRETE WALL SCHEDULE
S-606 - CONCRETE COLUMN ELEVATION
S-607 - CONCRETE COLUMN SCHEDULE
S-608 - CONCRETE BEAM DETAIL
S-609 - CONCRETE BEAM SCHEDULE

US Army Corps
of Engineers ®[illegible]

NOTES

1. SEE ARCHITECTURAL DRAWINGS FOR DIMENSIONS, ELEVATIONS AND DETAILS NOT SHOWN ON STRUCTURAL DRAWINGS.
2. SEE ARCHITECTURAL DRAWINGS FOR FLOOR SLOPE.
3. VERIFY WITH ARCHITECT/MECHANICAL FOR SIZE AND LOCATION OF OPENINGS.

US ARMY CORPS OF ENGINEERS JAPAN ENGINEER DISTRICT OKINAWA AREA OFFICE APO AF 96378-5132	DESIGNED BY: DRAWN BY: R. TANGNONAN CHECKED BY: W912HW-17-0-0003 SUBMITTED BY: J. UNO SIZE:	ISSUE DATE: SOLICITATION NO.: CONTRACT NO.: W912HW-17-0-0003
 S&M INTERNATIONAL, INC. 501 SUMNER STREET, SUITE 620		


Autodesk Docs: \Vehicle Maint Shop Kadena\511758 TEMF STRUC.INI

File Path:

Plot Date: 12/16/2025 3:36:44 PM

CLIN 0002

GRAPHIC SCALE

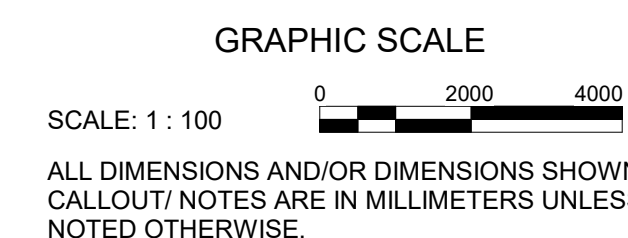

APO AP 96343-5010
FY20 MCA PN77833 VEHICLE MAINTENANCE SHOP

ORGANIZATIONAL STORAGE - BUILDING SECTIONS (CLIN 0002)

SHEET ID
OS
S-B30

INTERMEDIATE DESIGN

1 2 3 4 5 6 7 8 9 10 11 12 13 14 15 16 17 18 19 20 21

P

O

N

M

L

K

J

I

H

G

F

E

D

C

B

A

DRAFT

A

SECTION

SCALE 1 : 20

4

SECTION

SCALE 1 : 20

CLIN 0002

GRAPHIC SCALE

SCALE: 1 : 20

0 400 800

ALL DIMENSIONS AND/OR DIMENSIONS SHOWN
CALLOUT/NOTES ARE IN MILLIMETERS UNLESS
NOTED OTHERWISE.



**US Army Corps
of Engineers ®**

[illegible]

US ARMY CORPS OF ENGINEERS JAPAN ENGINEER DISTRICT OKINAWA AREA OFFICE APO AP 96376-5132			DESIGNED BY: A. MALLARI	ISSUE DATE: JUNE 2018
	SSFM INTERNATIONAL, INC. 500 KALANIANAʻOHE BLVD HONOLULU, HAWAII 96817		SOLICITATION NO.: R. TANGONAN	CONTRACT NO.: W912HW-17-D-0003

AP0 AP 96343-5010
FY20 MCA PN77833 VEHICLE MAINTENANCE SHOP
ORGANIZATIONAL STORAGE - SECTIONS AND
DETAILS (CLIN 0002)

SHEET ID
OS
S-B501



Autodesk Docs: //Vehicle Maint Shop Kadena/511758_TMF_STRUC.nvt

File Path:

12/16/2025 3:36:15 PM

Plot Date:

INTERMEDIATE DESIGN

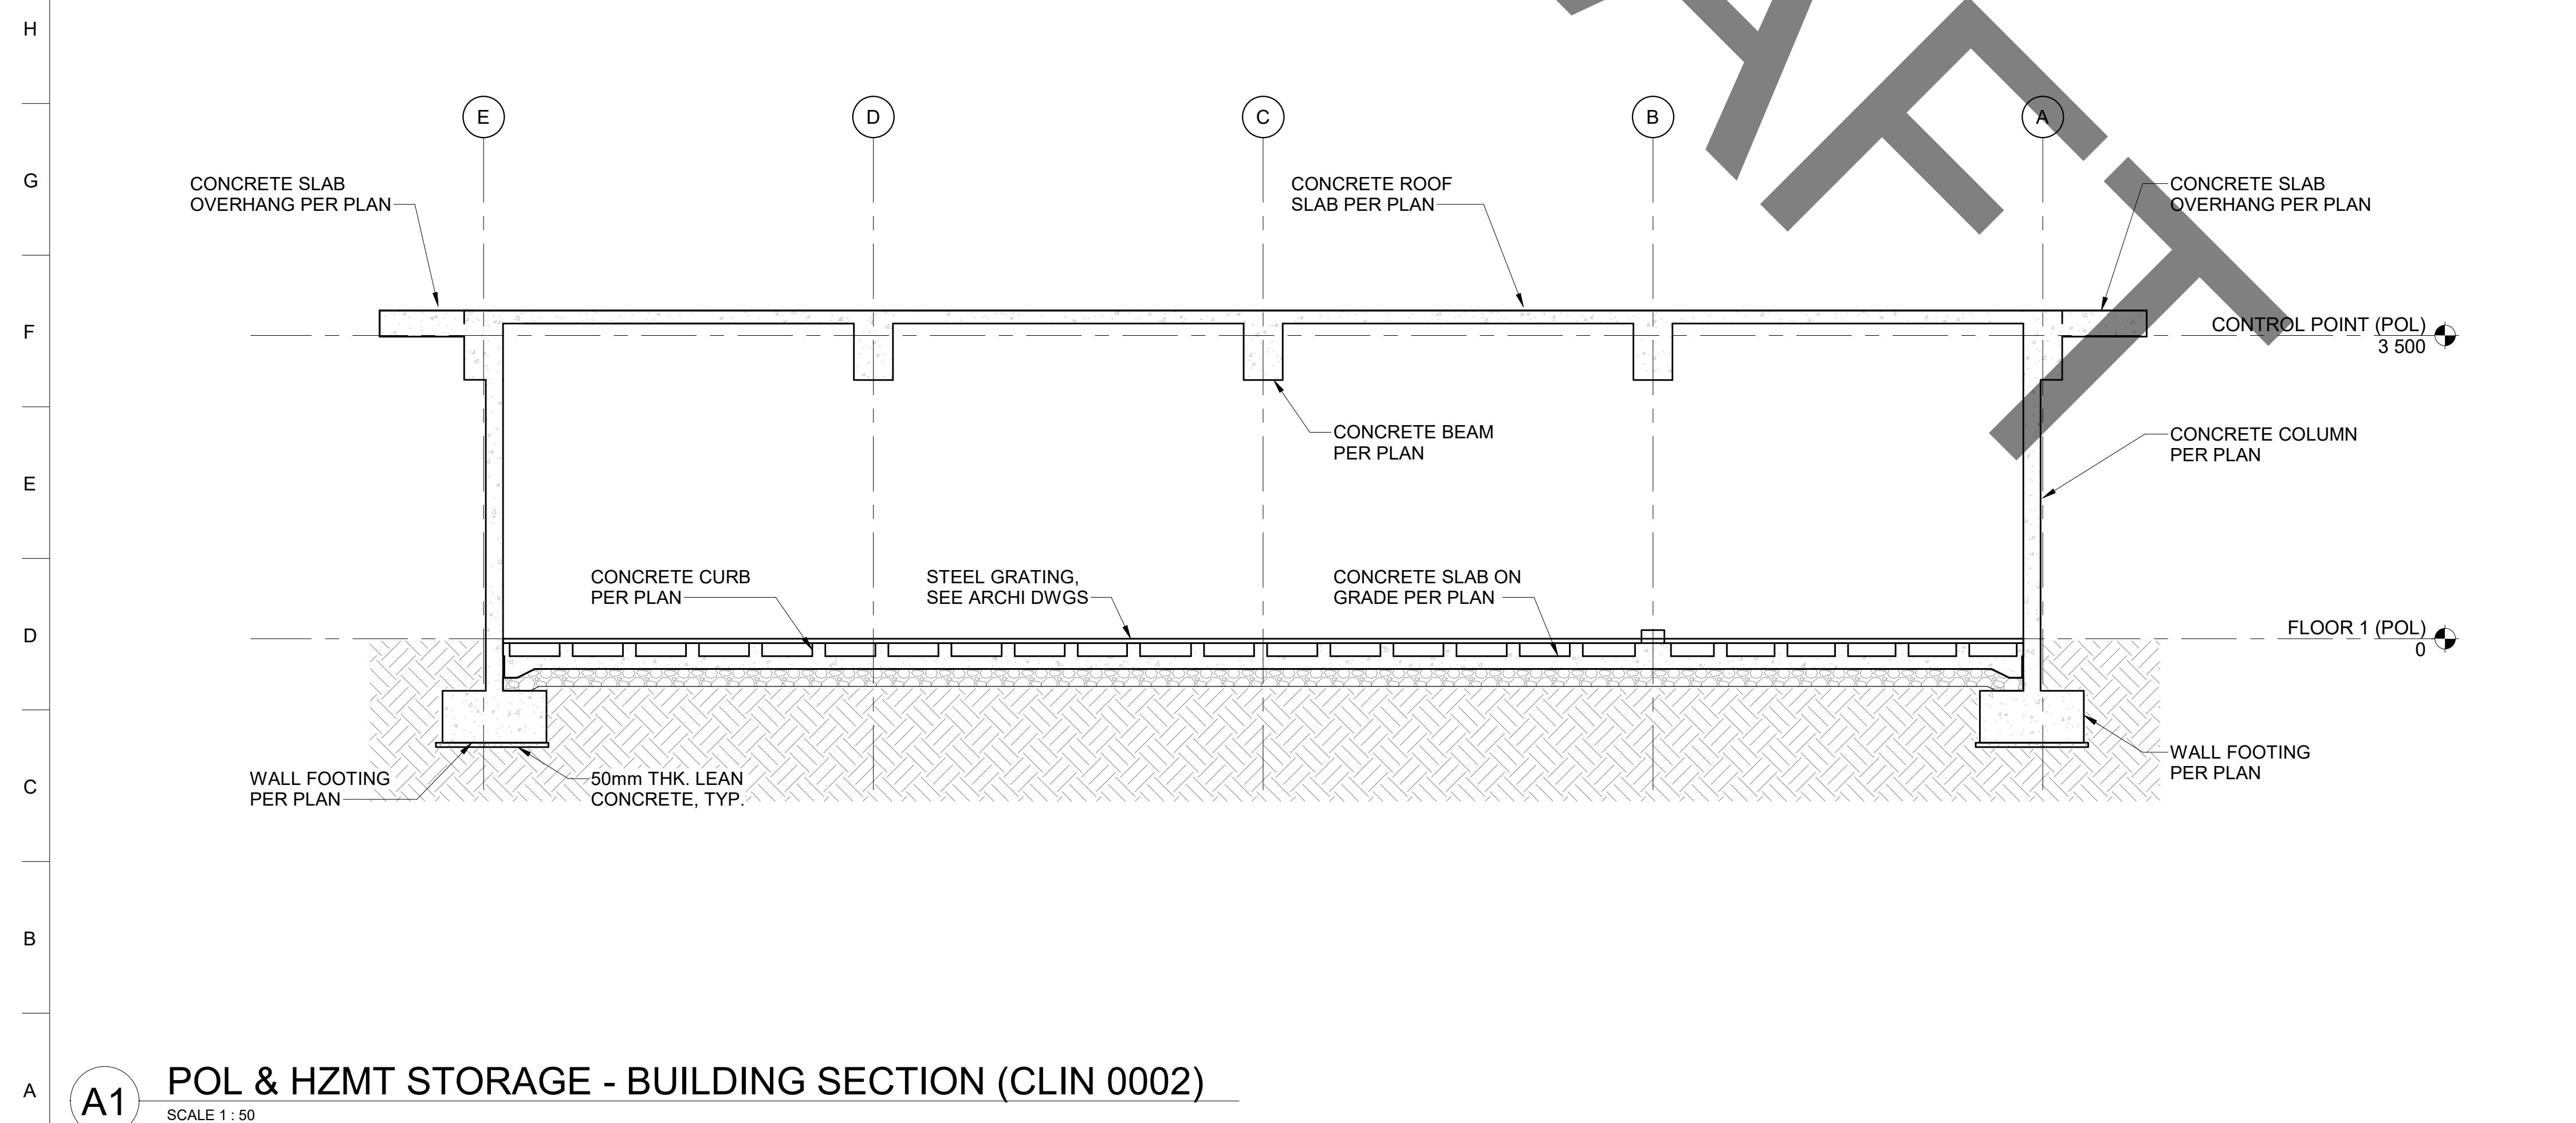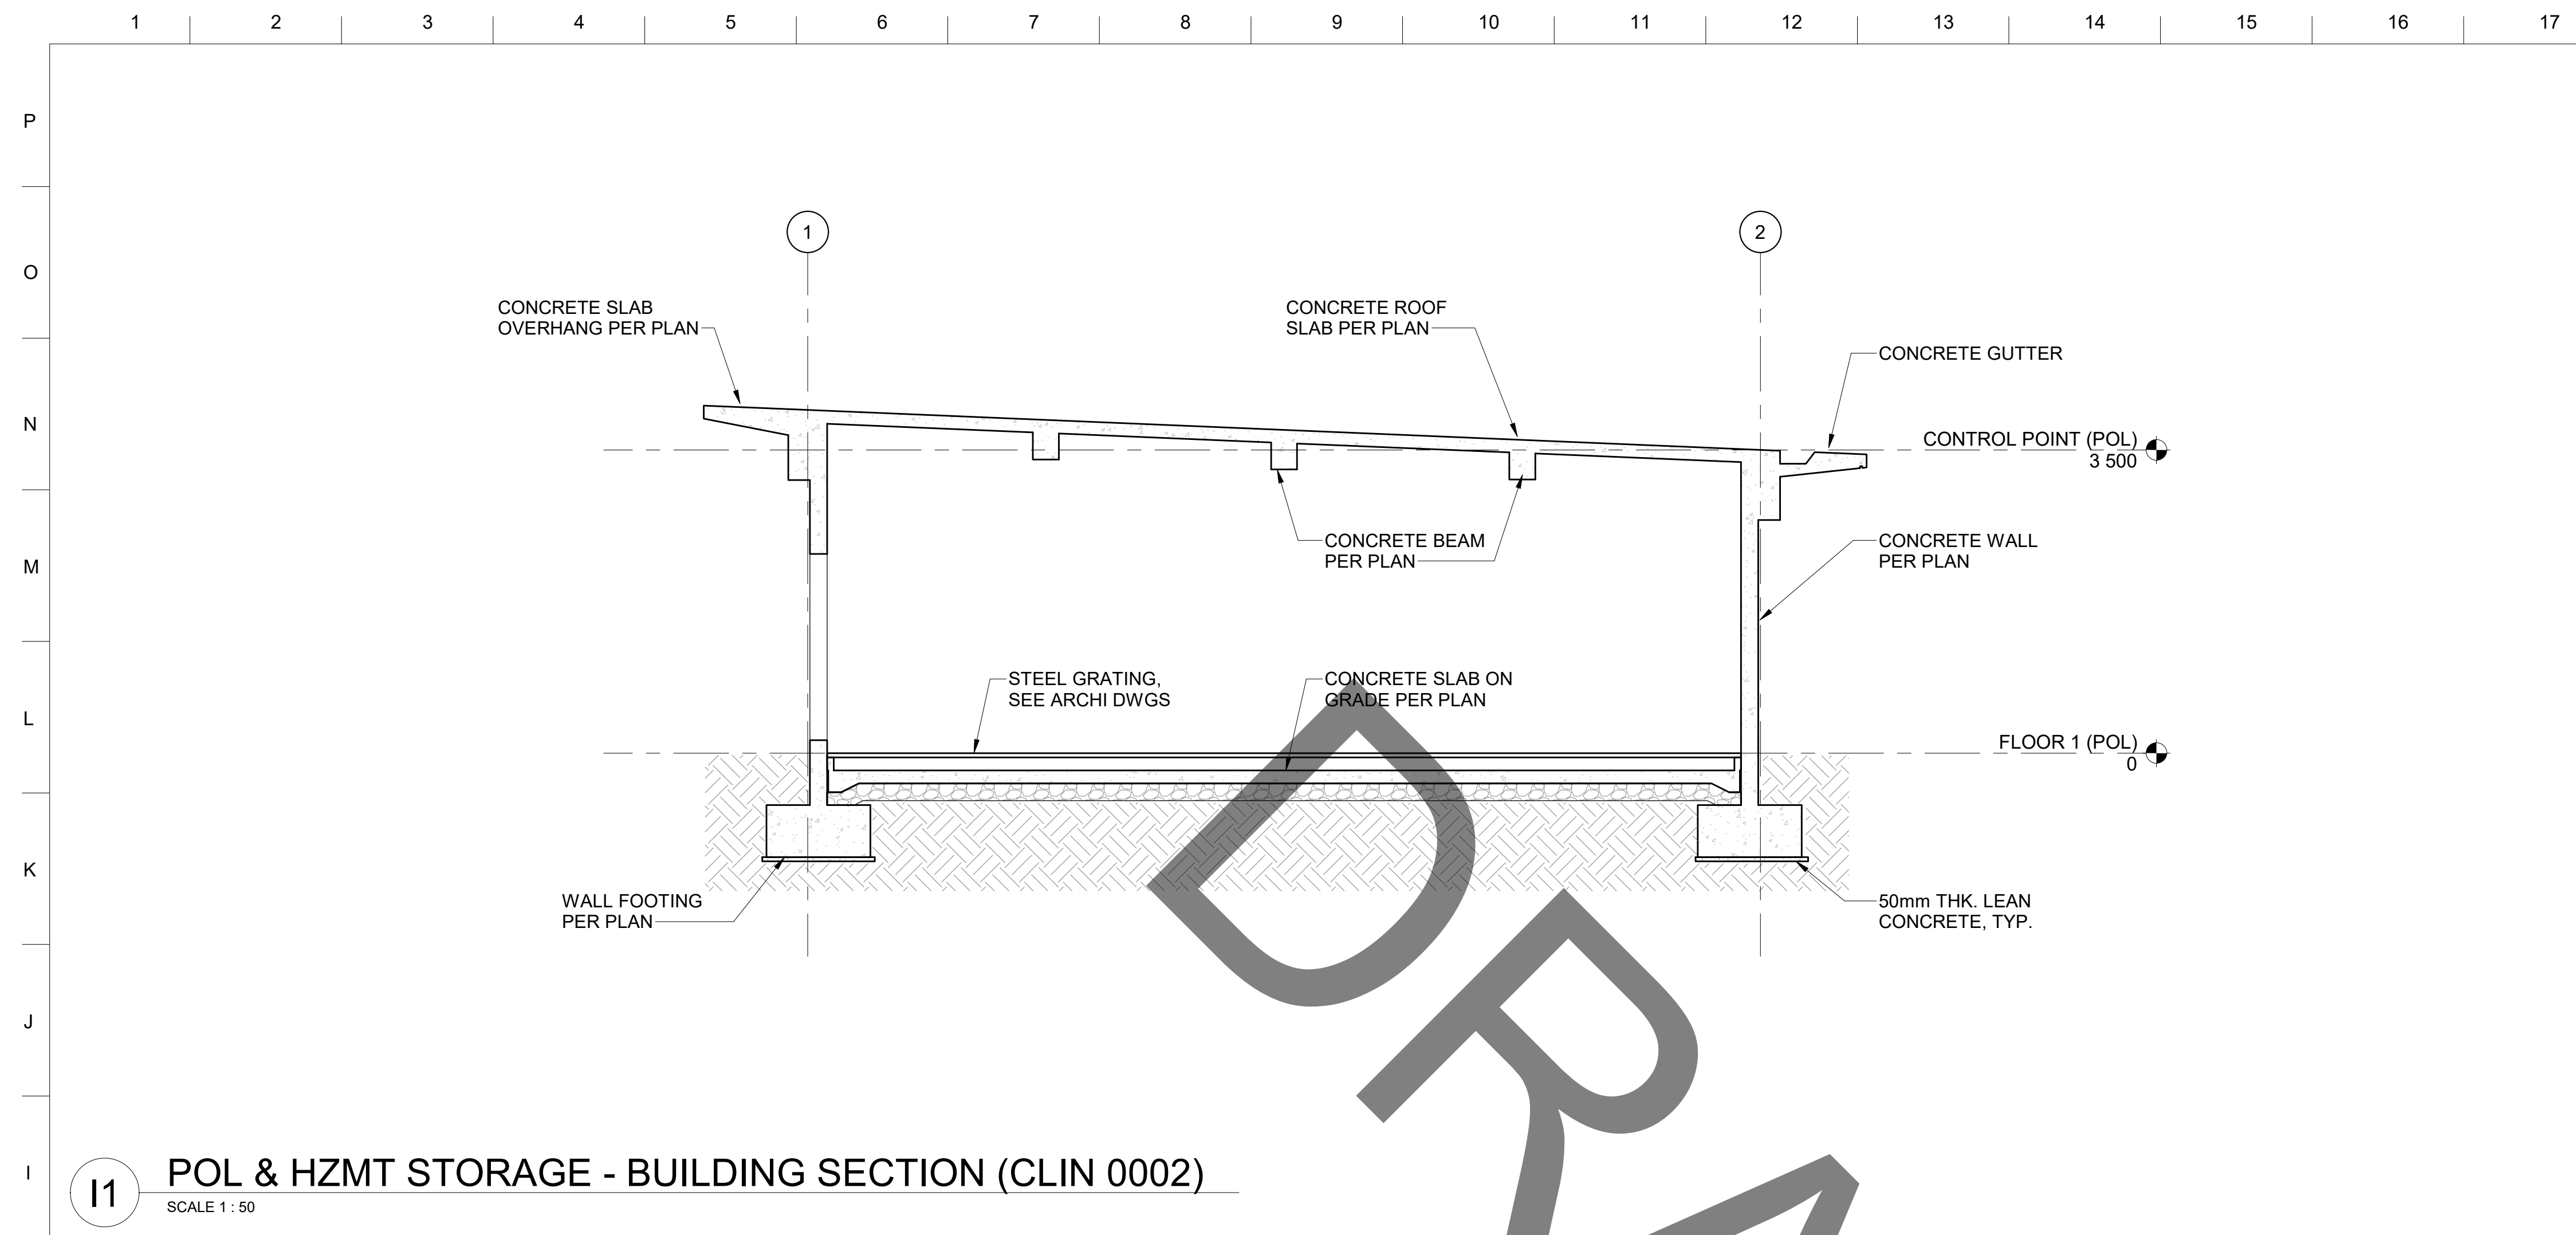

REFERENCE DRAWINGS

- S-001 - GENERAL NOTES
- S-002 - DESIGN DATA, DESIGN CODES AND STANDARDS, ABBREVIATION
- S-501 - TYPICAL REINFORCING STEEL DETAILS
- S-502 - TYPICAL CONCRETE DETAILS
- S-604 - CONCRETE FOOTING SCHEDULE
- S-605 - CONCRETE WALL SCHEDULE
- S-606 - CONCRETE COLUMN ELEVATION
- S-607 - CONCRETE COLUMN SCHEDULE
- S-608 - CONCRETE BEAM DETAIL
- S-609 - CONCRETE BEAM SCHEDULE

NOTES

1. SEE ARCHITECTURAL DRAWINGS FOR DIMENSIONS, ELEVATIONS AND DETAILS NOT SHOWN ON STRUCTURAL DRAWINGS.
2. SEE ARCHITECTURAL DRAWINGS FOR FLOOR SLOPE.
3. VERIFY WITH ARCHITECT/MECHANICAL FOR SIZE AND LOCATION OF OPENINGS.

US Army Corps
of Engineers ®[illegible]

US ARMY CORPS OF ENGINEERS JAPAN ENGINEER DISTRICT OKINAWA AREA OFFICE APO AF 96378-5132	DESIGNED BY: R. T. JUNG DRAWN BY: R. TANGNONAN CHECKED BY: R. TANGNONAN SUBMITTED BY: J. UNO SIZE:	ISSUE DATE: SOLICITATION NO.: CONTRACT NO.: W912HN-17-D-0003
SSM SSM INTERNATIONAL, INC. 501 SUMNER STREET, SUITE 620		

	1	2	52
--	---	---	---	---	---	---	---	---	---	----	----	-----	-----	----

1	2	
---	---	---	---	---	---	---	---	---	----	----	-----	-----	

☐ Yes ☐ No

CLIN 0002

GRAPHIC SCALE

0 2000 4000


SCALE: 1 : 100



ALL DIMENSIONS AND/OR DIMENSIONS SHOWN IN
CALLOUT/ NOTES ARE IN MILLIMETERS UNLESS
NOTED OTHERWISE.

APO AP 96343-5010
 FY20 MCA PN77833 VEHICLE MAINTENANCE SHOP
 POL & HAZMAT STORAGE BUILDING SECTIONS
 (CLIN 0002)

SHEET ID
POL &
HZMT
S-C301

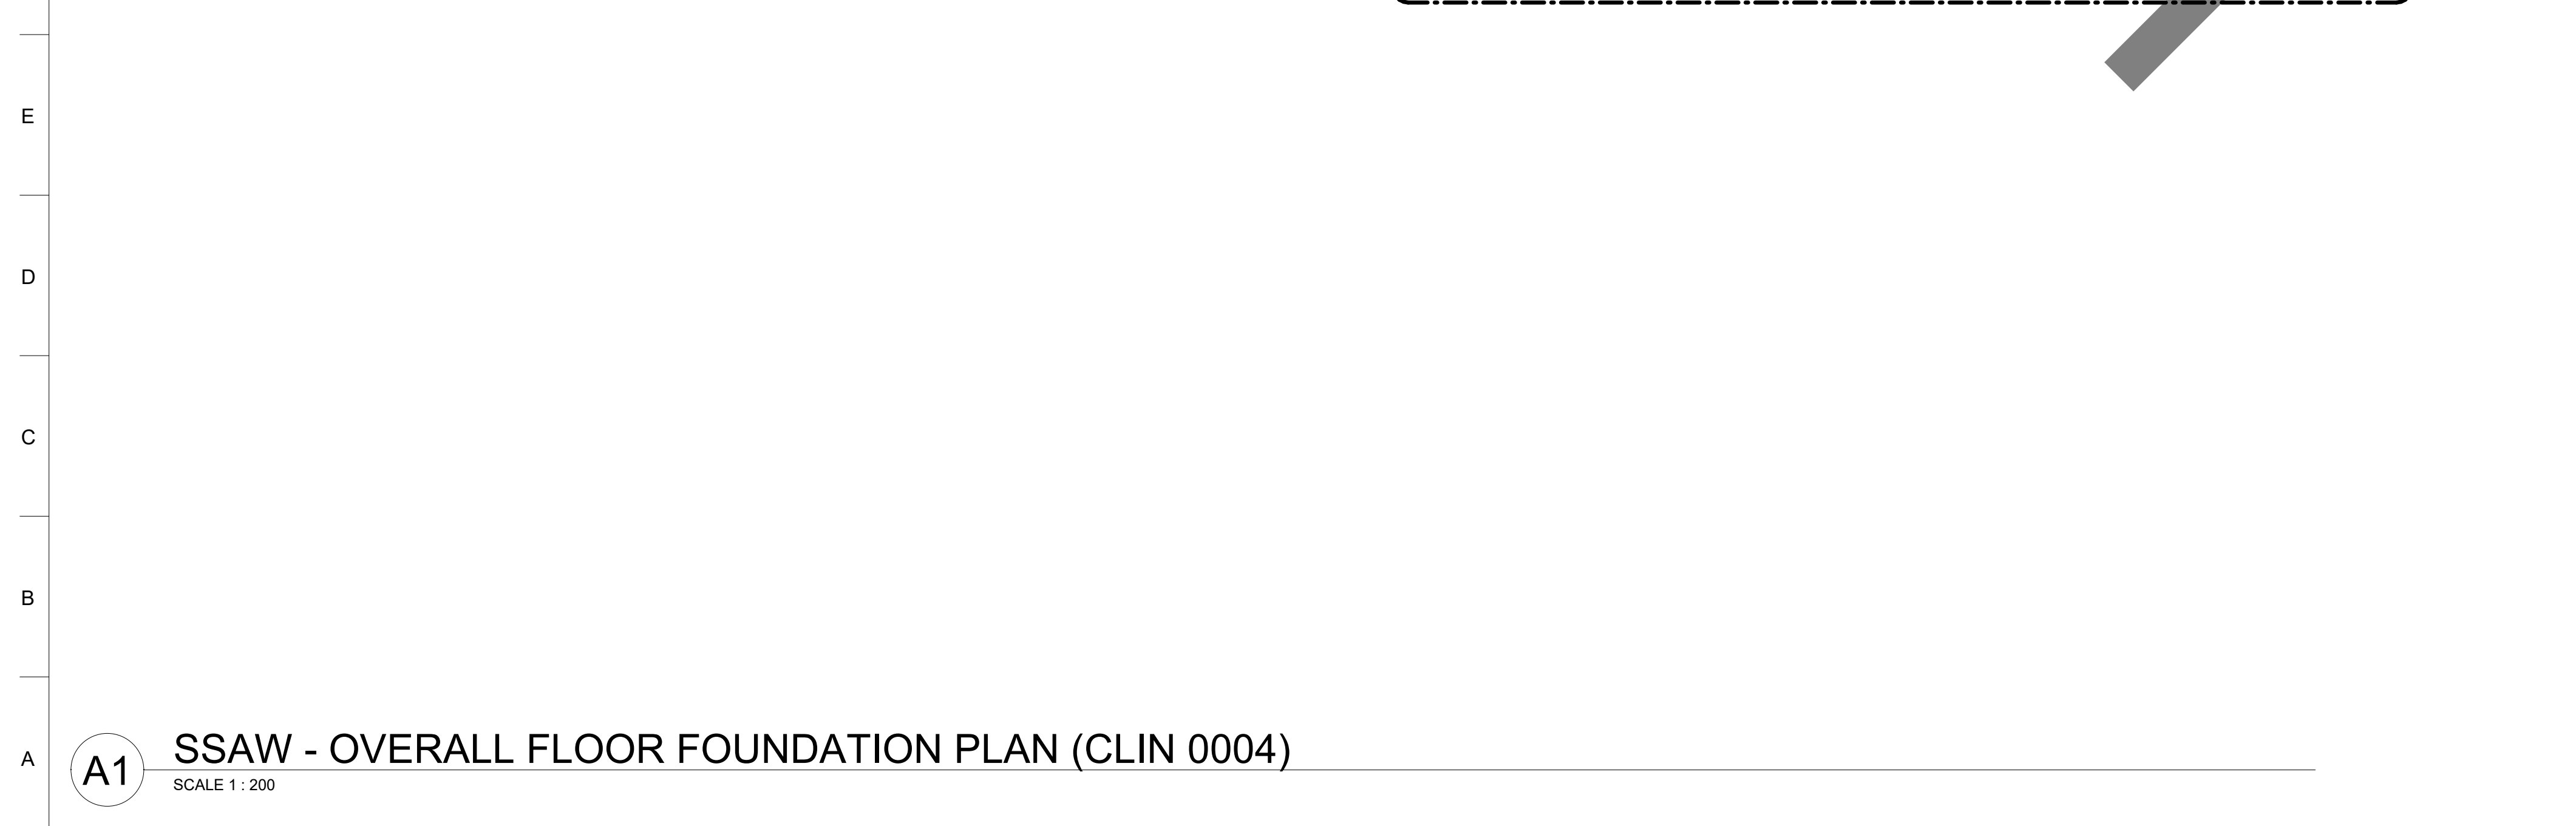

- S-001 - GENERAL NOTES
- S-002 - DESIGN DATA, DESIGN CODES AND STANDARDS, ABBREVIATION
- S-501 - TYPICAL REINFORCING STEEL DETAILS
- S-502 - TYPICAL CONCRETE DETAILS
- S-601 - CONCRETE PILE CAP SCHEDULE
- S-602 - CONCRETE PILE SCHEDULE
- S-603 - CONCRETE GRADE BEAM AND TIE BEAM SCHEDULE
- S-604 - CONCRETE FOOTING SCHEDULE
- S-605 - CONCRETE WALL SCHEDULE
- S-606 - CONCRETE COLUMN ELEVATION
- S-607 - CONCRETE COLUMN SCHEDULE
- S-608 - CONCRETE BEAM DETAIL
- S-609 - CONCRETE BEAM SCHEDULE

C.J. DENOTES CONSTRUCTION JOINT
S.J. DENOTES SAWCUT JOINT

CLIN 0004

GRAPHIC SCALE

PLAN
NORTH

GRAPHIC SCALE

SCALE: 1 : 100

020004000

ALL DIMENSIONS AND/OR DIMENSIONS SHOWN IN
CALLOUT/ NOTES ARE IN MILLIMETERS UNLESS
NOTED OTHERWISE.

 US Army Corps of Engineers ®		DATE	
MARK		DESCRIPTION	
DESIGNED BY: E. YAO		ISSUE DATE: JUNE 2018	
DRAWN BY: J. HONGMAN		SOLICITATION NO.:	
CHECKED BY: J. UNO		CONTRACT NO.:	
SUBMITTED BY: J. UNO		W912HV-17-D-0003	
US ARMY CORPS OF ENGINEERS JAPAN ENGINEER DISTRICT OKINAWA AREA OFFICE APO AP 96376-5132		ANSI D	
sspm INTERNATIONAL		SSPM INTERNATIONAL, INC 5055 KALANANUOULI DRIVE, #220 HONOLULU, HAWAII 96817	
SSAW - OVERALL FLOOR FOUNDATION PLAN (CLIN 0004)			
SHEET ID SSAW S-D101			



REFERENCE DRAWINGS

- S-001 - GENERAL NOTES
- S-002 - DESIGN DATA, DESIGN CODES AND STANDARDS, ABBREVIATION
- S-501 - TYPICAL REINFORCING STEEL DETAILS
- S-502 - TYPICAL CONCRETE DETAILS
- S-503 - TYPICAL STEEL DECK DETAILS
- S-504 - TYPICAL STEEL NOTES AND DETAILS
- S-605 - CONCRETE WALL SCHEDULE
- S-606 - CONCRETE COLUMN ELEVATION
- S-607 - CONCRETE COLUMN SCHEDULE
- S-608 - CONCRETE BEAM DETAIL
- S-609 - CONCRETE BEAM SCHEDULE

CLIN 0004

GRAPHIC SCALE


PLAN
NORTH


GRAPHIC SCALE

0 4000 8000

SCALE: 1 : 200

ALL DIMENSIONS AND/OR DIMENSIONS SHOWN IN
CALLOUT/ NOTES ARE IN MILLIMETERS UNLESS
NOTED OTHERWISE.

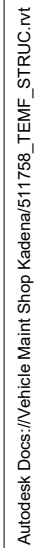

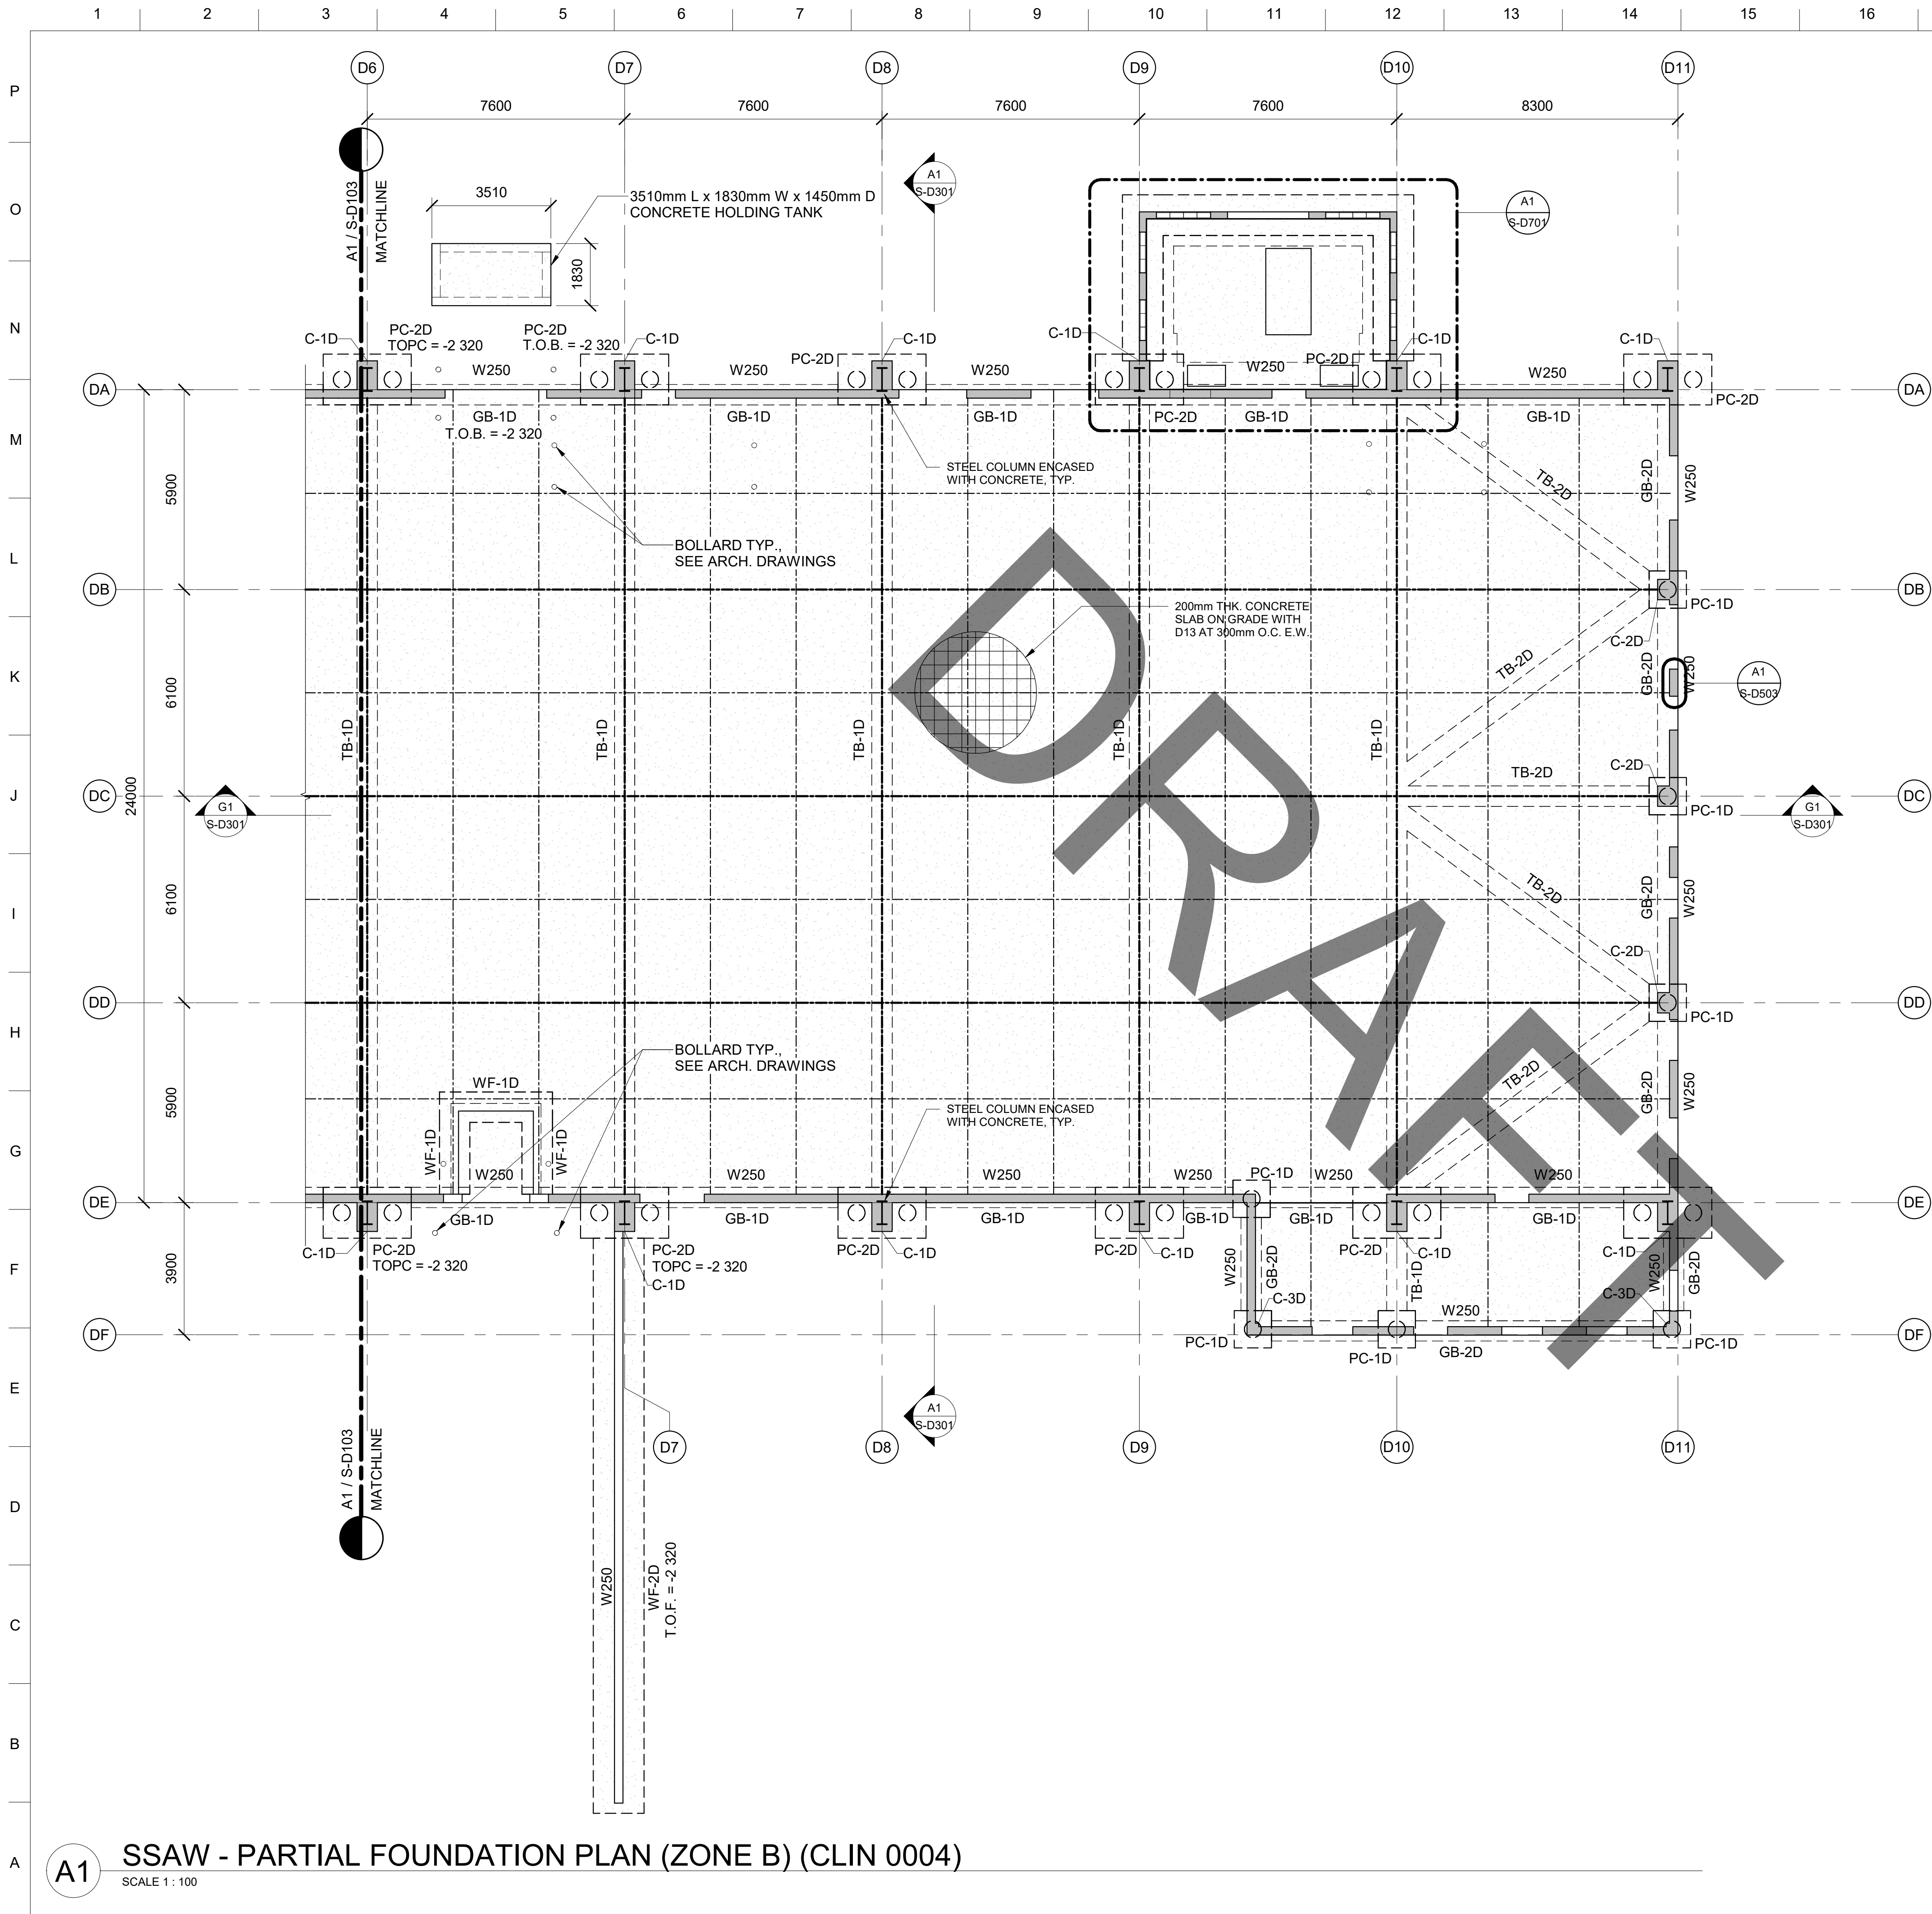

A1 SSAW - PARTIAL FOUNDATION PLAN (ZONE B) (CLIN 0004)

SCALE 1 : 100

REFERENCE DRAWINGS

- S-001 - GENERAL NOTES
- S-002 - DESIGN DATA, DESIGN CODES AND STANDARDS, ABBREVIATION
- S-501 - TYPICAL REINFORCING STEEL DETAILS
- S-502 - TYPICAL CONCRETE DETAILS
- S-601 - CONCRETE PILE CAP SCHEDULE
- S-602 - CONCRETE PILE SCHEDULE
- S-603 - CONCRETE GRADE BEAM AND TIE BEAM SCHEDULE
- S-604 - CONCRETE FOOTING SCHEDULE
- S-605 - CONCRETE WALL SCHEDULE
- S-606 - CONCRETE COLUMN ELEVATION
- S-607 - CONCRETE COLUMN SCHEDULE

LEGEND

- | | |
|------|----------------------------|
| PC-X | DENOTES PILE CAP |
| GB-X | DENOTES GRADE BEAM |
| TB-X | DENOTES TIE BEAM |
| W-X | DENOTES CONCRETE WALL |
| C-X | DENOTES CONCRETE COLUMN |
| C.J. | DENOTES CONSTRUCTION JOINT |
| S.J | DENOTES SAWCUT JOINT |


NOTES

- SEE ARCHITECTURAL DRAWINGS FOR DIMENSIONS, ELEVATIONS AND DETAILS NOT SHOWN ON STRUCTURAL DRAWINGS.
- SEE ARCHITECTURAL DRAWINGS FOR FLOOR SLOPE.
- VERIFY WITH ARCHITECT/MECHANICAL FOR SIZE AND LOCATION OF OPENINGS.
- THICKNESS OF CONCRETE SLABS SHOWN ARE MINIMUM AND MUST BE MAINTAINED AT SLOPED PORTION.
- SEE CIVIL DRAWINGS FOR FINISH FLOOR ELEVATION.
- TYP TOP OF SLAB-ON-GRADE EL = 0 UNO
- TYP TOP OF GRADE BEAM/TIE BEAM EL = -1100 UNO
- TYP TOP OF PILE CAP EL = -1100 UNO
- SEE A10/S-605 FOR W200 TOP OF WALL CONNECTION TO FLOOR/ROOF SLAB.


CLIN 0004

KEYPLAN

SSAW
N.T.S.

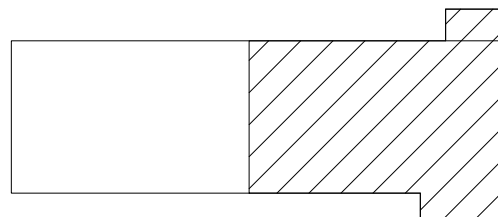

GRAPHIC SCALE

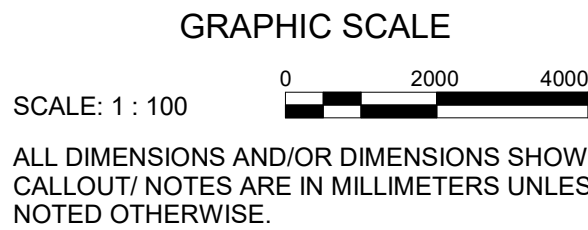

US Army Corps
of Engineers ®

DATE	DESCRIPTION	MARK

ISSUE DATE: JUNE 2018	SOLICITATION NO.: 	CONTRACT NO.: W72AW-17-D-0003
DESIGNED BY: E. YAO	CHECKED BY: R. TANGONAN	SUBMITTED BY: J. UNO
DRAWN BY: R. TANGONAN	APPROVED BY: 	SIZE: ANSI D
US ARMY CORPS OF ENGINEERS JAPAN ENGINEER DISTRICT OKINAWA AREA OFFICE APO AP 96376-5132	SSAW INTERNATIONAL, INC. 507 SUMNER STREET, SUITE 620 HONOLULU, HAWAII 96817	


APO AP 96343-5010
FY20 MCA PN77833 VEHICLE MAINTENANCE SHOP

SSAW - PARTIAL FOUNDATION PLAN - (ZONE B)
(CLIN 0004)

SHEET ID
SSAW
S-D104

INTERMEDIATE DESIGN

Plot Date: 12/16/2025 3:36:59 PM File Path: AutoCAD Docs \Vehicle Maint Shop Kadena\511796_TEMPL_STRUC.dwt

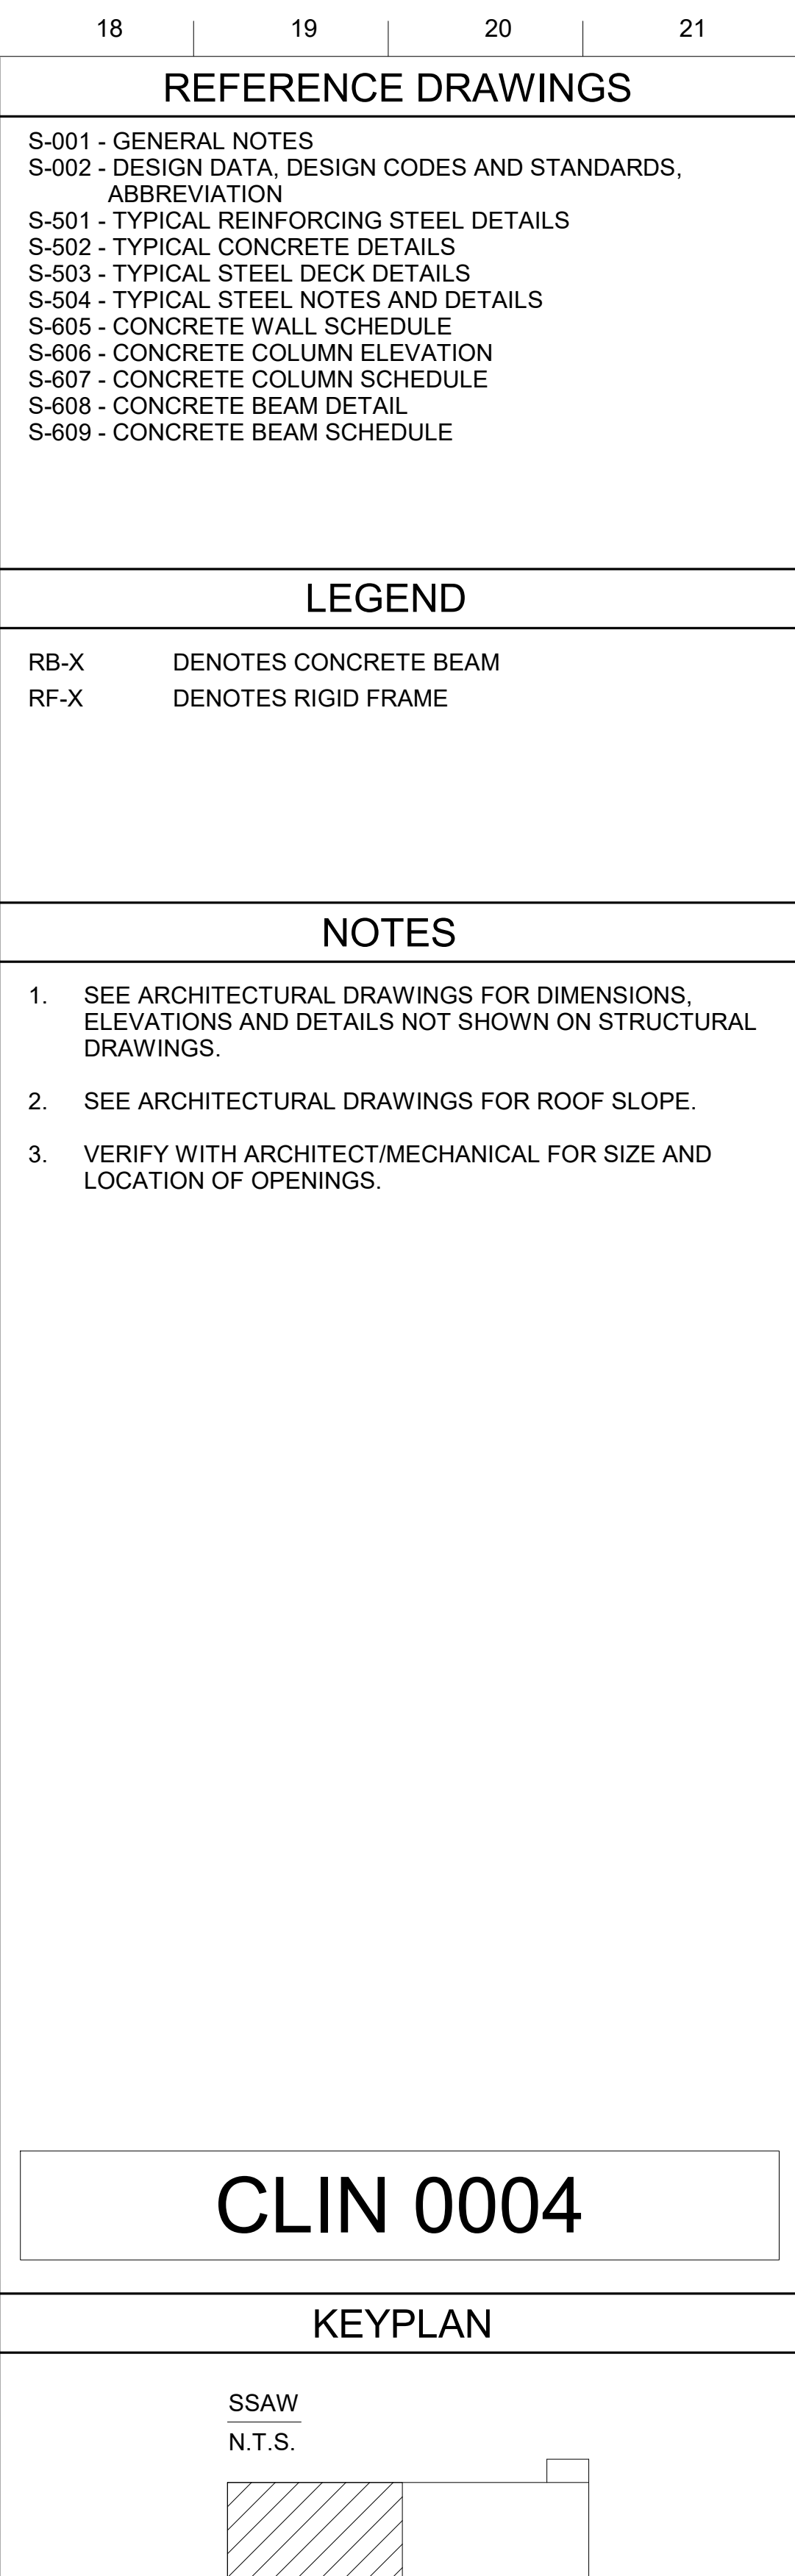

REFERENCE DRAWINGS

- S-001 - GENERAL NOTES
- S-002 - DESIGN DATA, DESIGN CODES AND STANDARDS, ABBREVIATION
- S-501 - TYPICAL REINFORCING STEEL DETAILS
- S-502 - TYPICAL CONCRETE DETAILS
- S-503 - TYPICAL STEEL DECK DETAILS
- S-504 - TYPICAL STEEL NOTES AND DETAILS
- S-605 - CONCRETE WALL SCHEDULE
- S-606 - CONCRETE COLUMN ELEVATION
- S-607 - CONCRETE COLUMN SCHEDULE
- S-608 - CONCRETE BEAM DETAIL
- S-609 - CONCRETE BEAM SCHEDULE

LEGEND	
RB-X	DENOTES CONCRETE BEAM
RF-X	DENOTES RIGID FRAME

NOTES

1. SEE ARCHITECTURAL DRAWINGS FOR DIMENSIONS, ELEVATIONS AND DETAILS NOT SHOWN ON STRUCTURAL DRAWINGS.
2. SEE ARCHITECTURAL DRAWINGS FOR ROOF SLOPE.
3. VERIFY WITH ARCHITECT/MECHANICAL FOR SIZE AND LOCATION OF OPENINGS.


[illegible]

DESIGNED BY: US ARMY CORPS OF ENGINEERS
 E. YACOB BY: JAPAN ENGINEER DISTRICT
 R. TANGONAN R. OKINAWA AREA OFFICE
 CHECKED BY: APO AF 96376-5132
 J. UNO
 SUBMITTED BY: SSM INTERNATIONAL INC.
 SIZE: SSP4 SUMNER STREET, SUITE 620
 HONOLULU HAWAII 96817
 ISSUE DATE: 501 SUMNER STREET, SUITE 620
 SOLICITATION NO.: HONOLULU HAWAII 96817
 CONTRACT NO.:
 W912HV-77-0-0003

SSAW - PARTIAL ROOF FRAMING PLAN - (ZONE A)
(CLIN 0004)

SHEET ID
SSAW
S-D105

INTERMEDIATE DESIGN Plot Date: 12/16/2025 3:37:02 PM File Path: Autodesk Docs:\Vehicle Maint Shop\Kadena511758_TEMF_STRUC.dwt

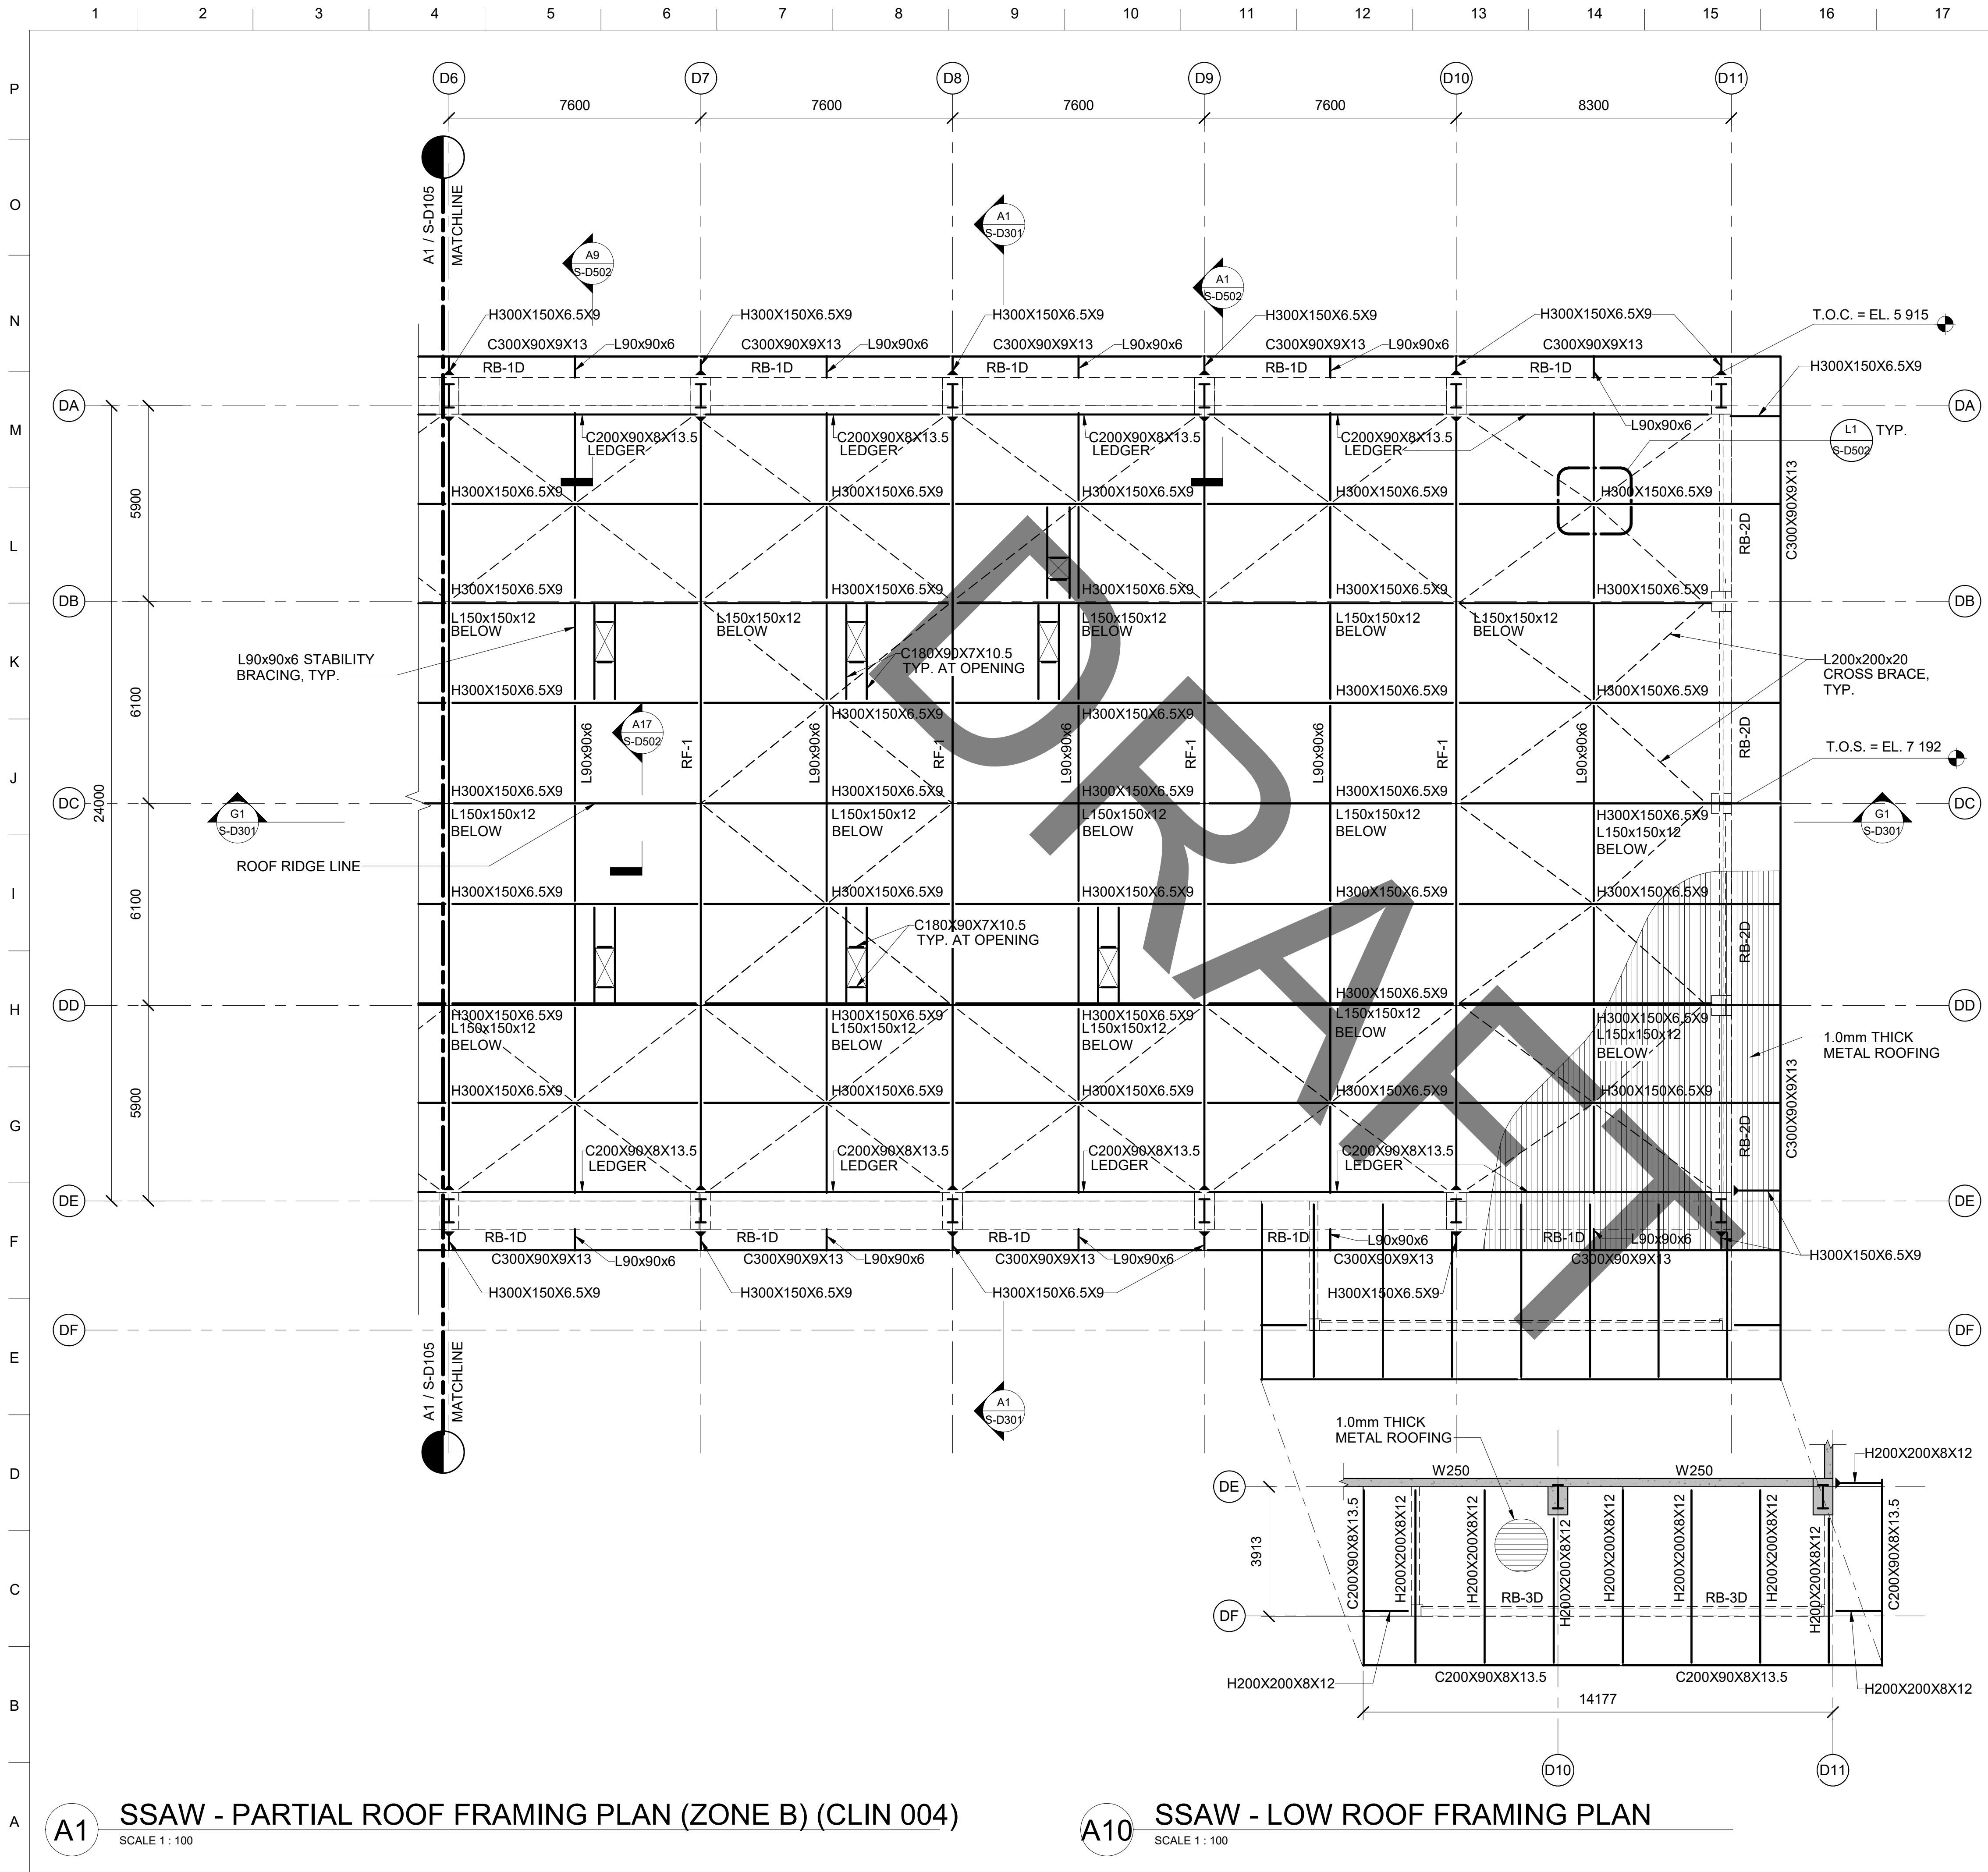

REFERENCE DRAWINGS	
S-001 - GENERAL NOTES	
S-002 - DESIGN DATA, DESIGN CODES AND STANDARDS, ABBREVIATION	
S-501 - TYPICAL REINFORCING STEEL DETAILS	
S-502 - TYPICAL CONCRETE DETAILS	
S-503 - TYPICAL STEEL DECK DETAILS	
S-504 - TYPICAL STEEL NOTES AND DETAILS	
S-605 - CONCRETE WALL SCHEDULE	
S-606 - CONCRETE COLUMN ELEVATION	
S-607 - CONCRETE COLUMN SCHEDULE	
S-608 - CONCRETE BEAM DETAIL	
S-609 - CONCRETE BEAM SCHEDULE	

LEGEND	
RB-X	DENOTES CONCRETE BEAM
RF-X	DENOTES RIGID FRAME

- | NOTES | |
|-------|---|
| 1. | SEE ARCHITECTURAL DRAWINGS FOR DIMENSIONS, ELEVATIONS AND DETAILS NOT SHOWN ON STRUCTURAL DRAWINGS. |
| 2. | SEE ARCHITECTURAL DRAWINGS FOR ROOF SLOPE. |
| 3. | VERIFY WITH ARCHITECT/MECHANICAL FOR SIZE AND LOCATION OF OPENINGS. |

US Army Corps of Engineers®

ISSUE DATE: JUNE 2018	SOLICITATION NO.: W912AV-17-D-0003	CONTRACT NO.: W912AV-17-D-0003	DATE
DESIGNED BY: E. YAO	DRAWN BY: R. TANGONAN	CHECKED BY: J. LINO	MARK
SUBMITTED BY: J. LINO			DESCRIPTION
SIZE: ANSI D			



US ARMY CORPS OF ENGINEERS
JAPAN ENGINEER DISTRICT
OKINAWA AREA OFFICE
APO AP 96343-5132

SSAW INTERNATIONAL, INC.
507 SUMNER STREET, SUITE 620
HONOLULU, HAWAII 96817

SSAW - PARTIAL ROOF FRAMING PLAN - (ZONE B)
(CLIN 0004)


SHEET ID
SSAW
S-D106

CLIN 0004

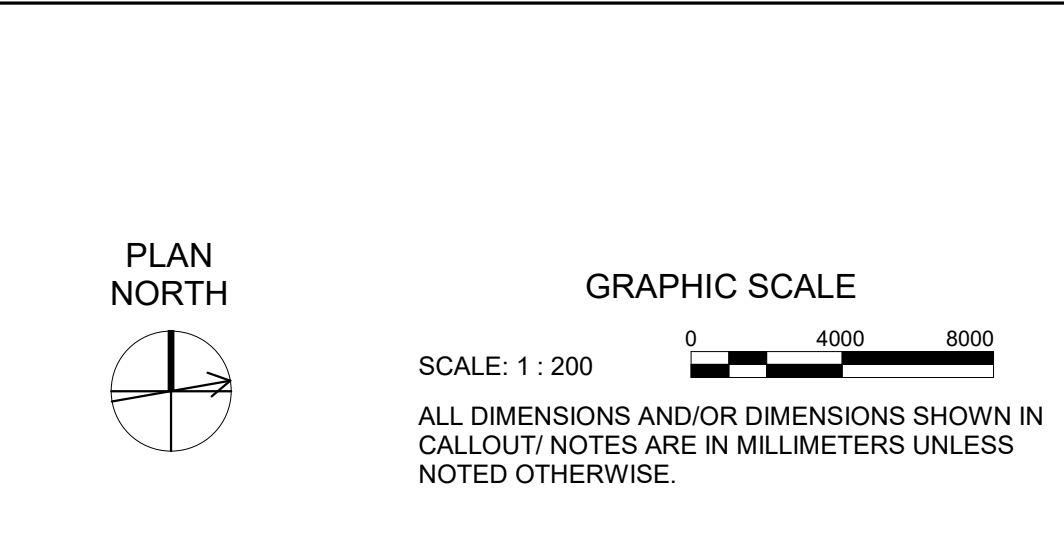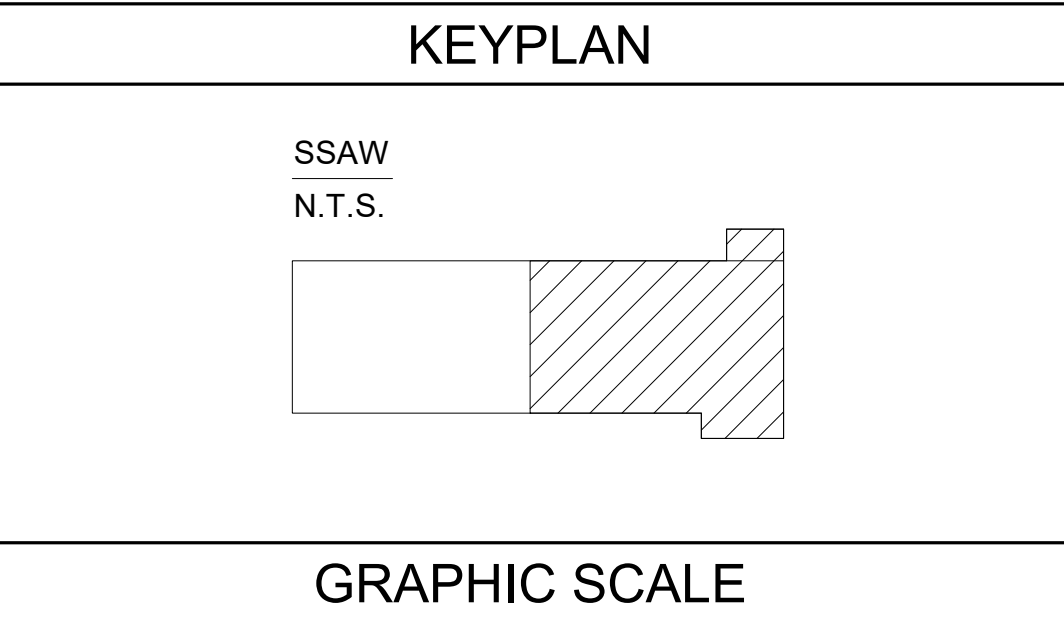


A10 SSaw - LOW ROOF FRAMING PLAN
SCALE 1 : 100


A1 SSaw - PARTIAL ROOF FRAMING PLAN (ZONE B) (CLIN 004)
SCALE 1 : 100

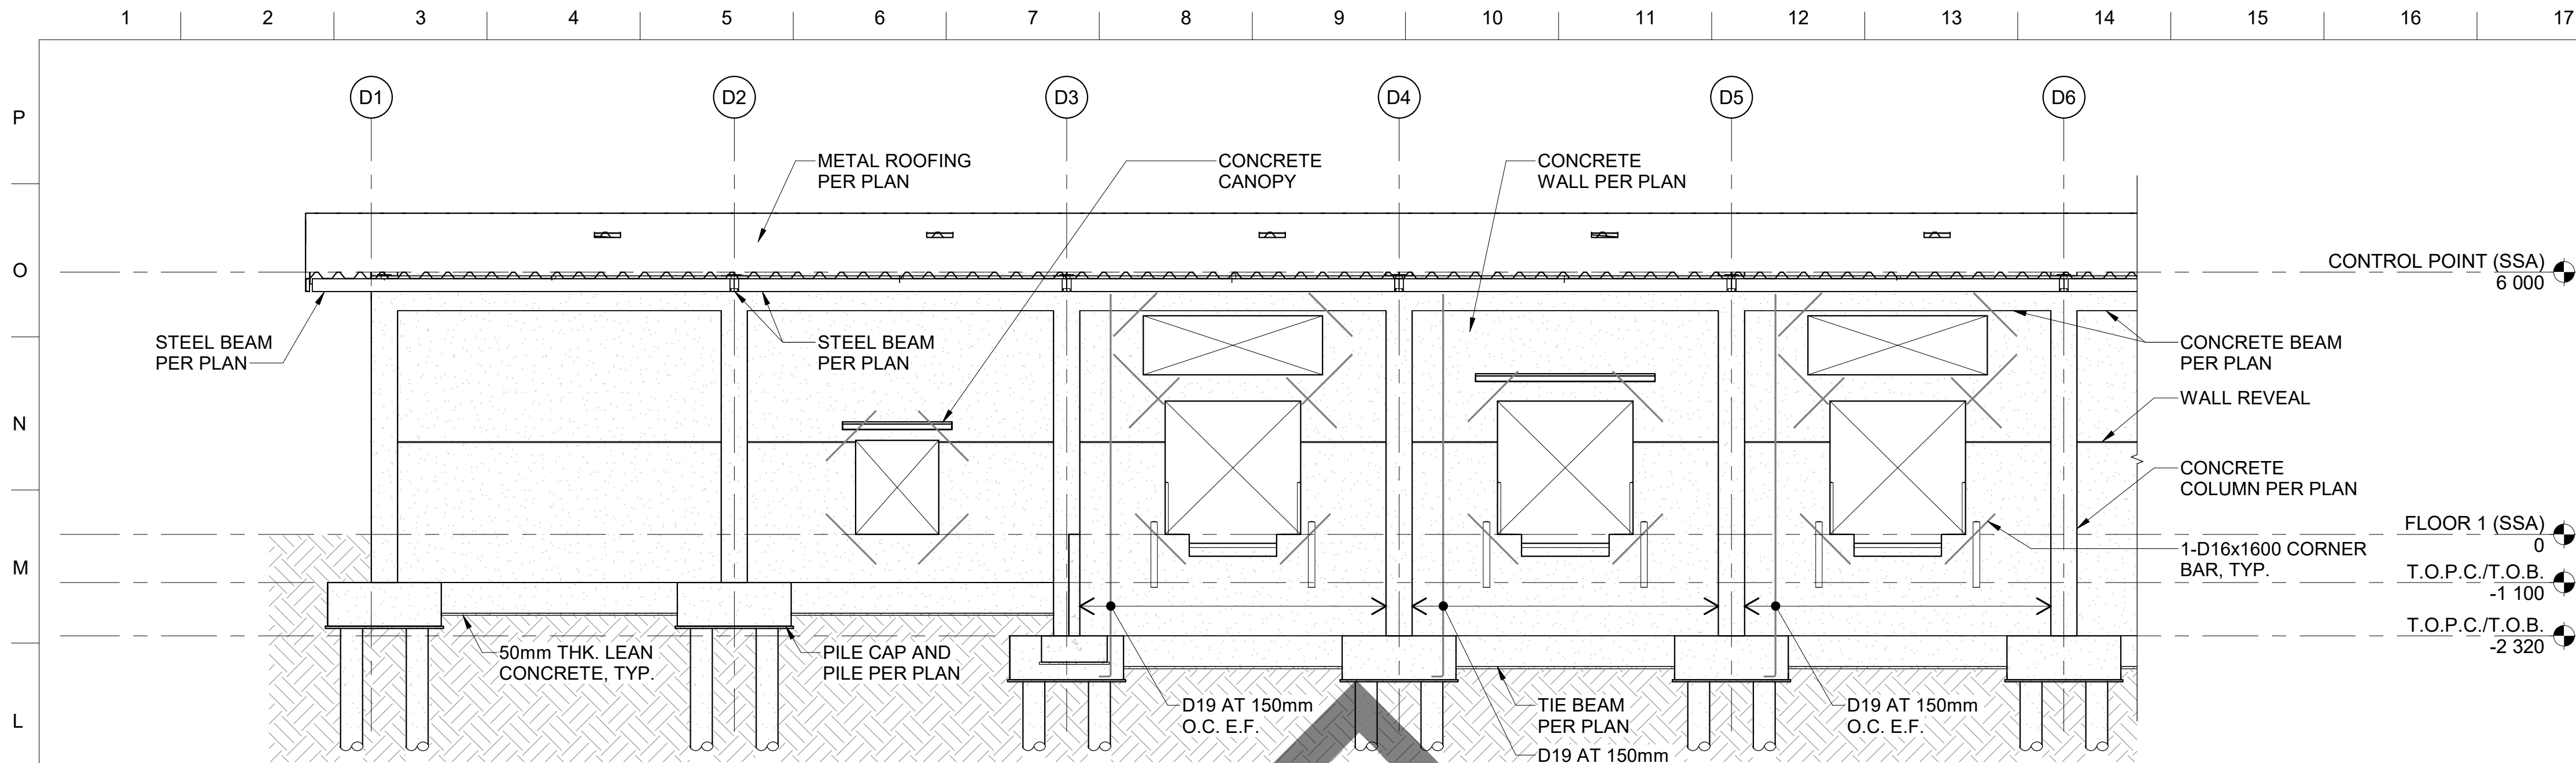

K1 SSAW - PARTIAL EXTERIOR ELEVATION - SOUTH (WEST) (CLIN 0004)
SCALE 1 : 100

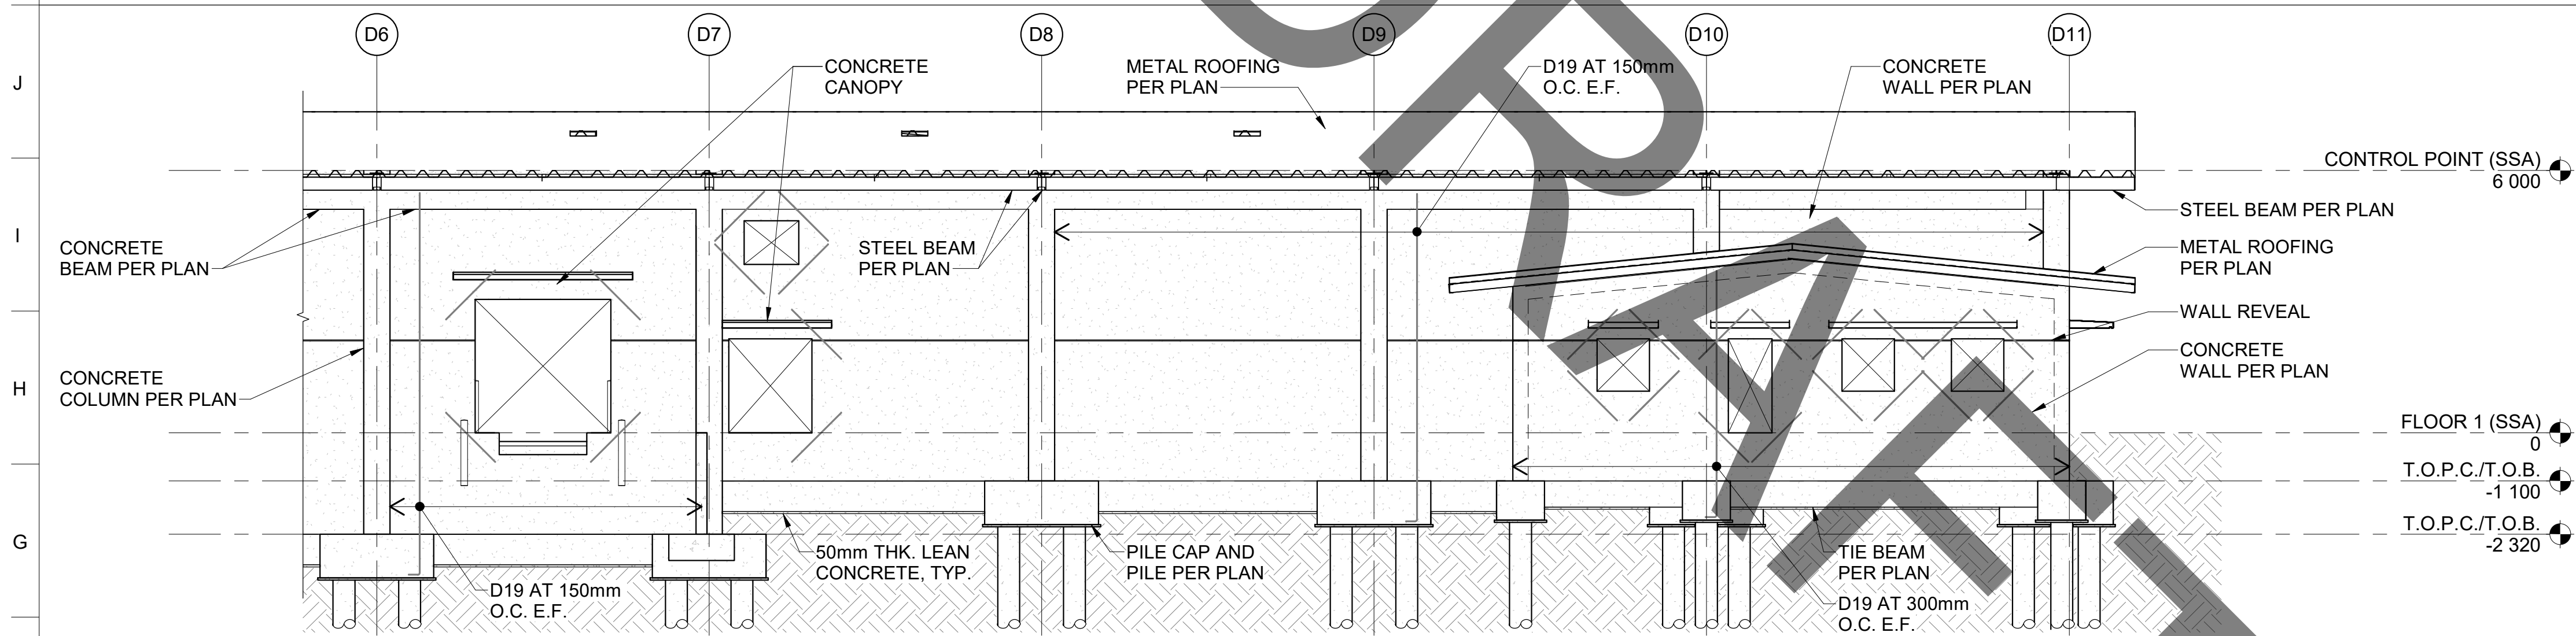

F1 SSAW - PARTIAL EXTERIOR ELEVATION - SOUTH (EAST) (CLIN 0004)
SCALE 1 : 100

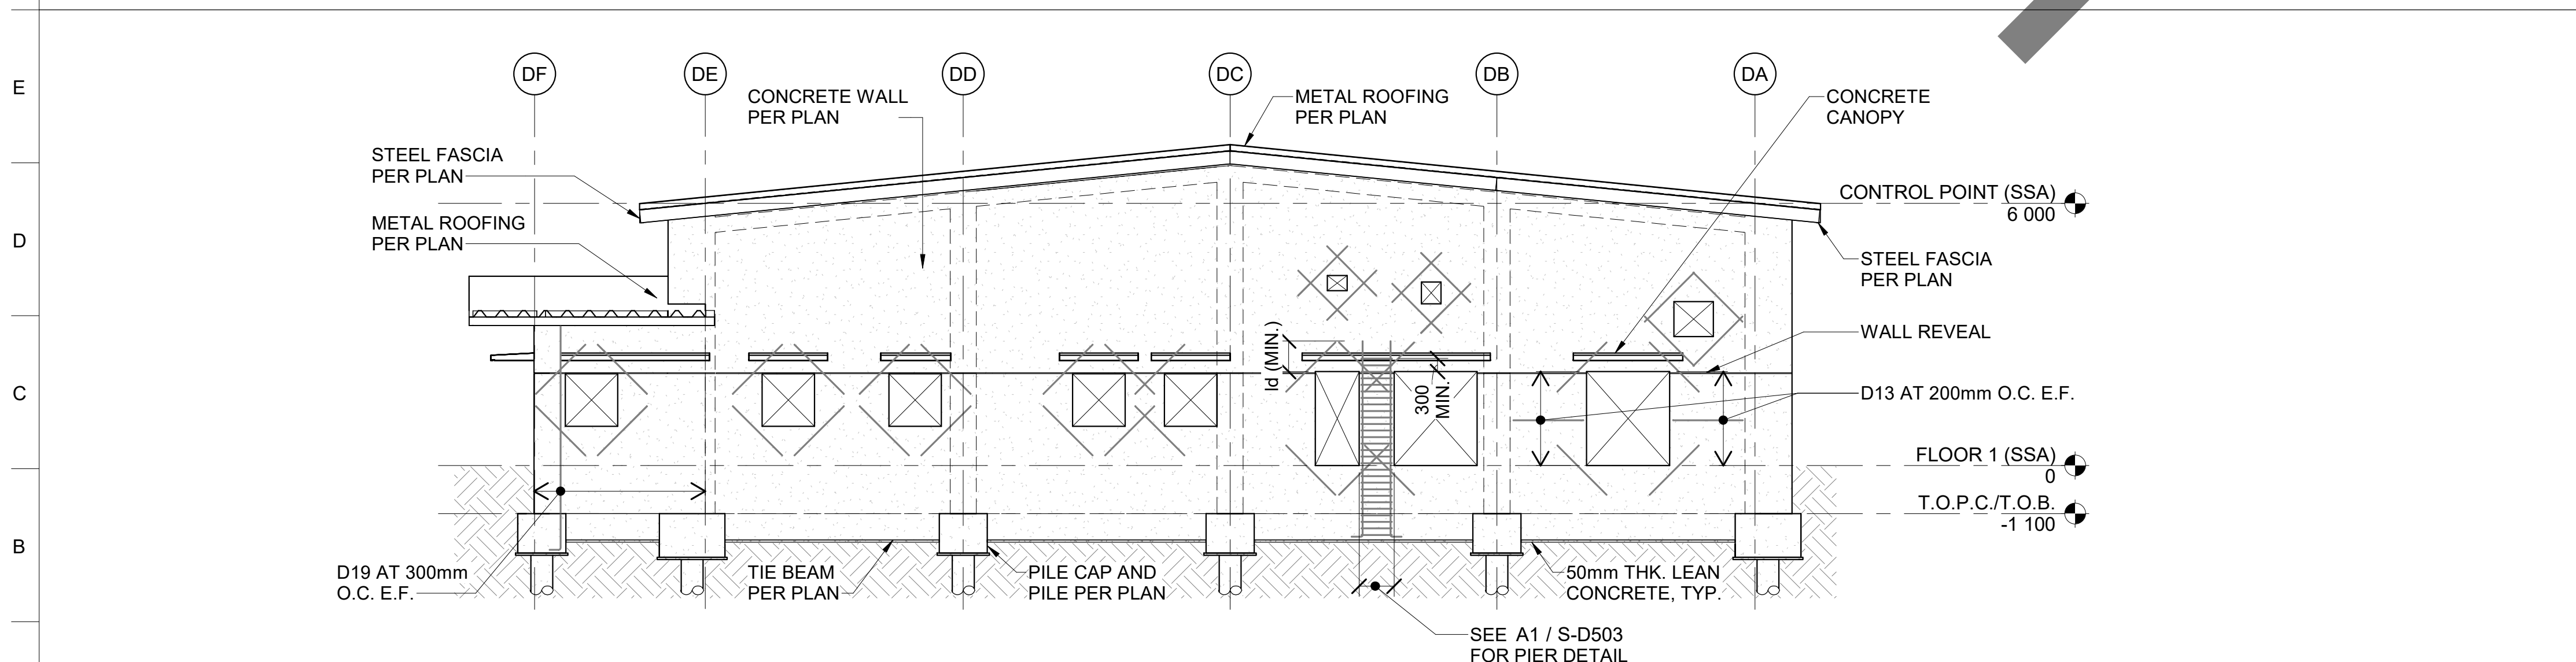

A1 SSAW - EXTERIOR ELEVATION - EAST (CLIN 0004)
SCALE 1 : 100

REFERENCE DRAWINGS


S-001 - GENERAL NOTES
S-002 - DESIGN DATA, DESIGN CODES AND STANDARDS, ABBREVIATION
S-501 - TYPICAL REINFORCING STEEL DETAILS
S-502 - TYPICAL CONCRETE DETAILS
S-601 - CONCRETE PILE CAP SCHEDULE
S-602 - CONCRETE PILE SCHEDULE
S-603 - CONCRETE GRADE BEAM AND TIE BEAM SCHEDULE
S-604 - CONCRETE FOOTING SCHEDULE
S-605 - CONCRETE WALL SCHEDULE
S-606 - CONCRETE COLUMN ELEVATION
S-607 - CONCRETE COLUMN SCHEDULE
S-608 - CONCRETE BEAM DETAIL
S-609 - CONCRETE BEAM SCHEDULE

NOTES

- SEE ARCHITECTURAL DRAWINGS FOR DIMENSIONS, ELEVATIONS AND DETAILS NOT SHOWN ON STRUCTURAL DRAWINGS.
- SEE ARCHITECTURAL DRAWINGS FOR FLOOR SLOPE.
- VERIFY WITH ARCHITECT/MECHANICAL FOR SIZE AND LOCATION OF OPENINGS.

CLIN 0004

GRAPHIC SCALE

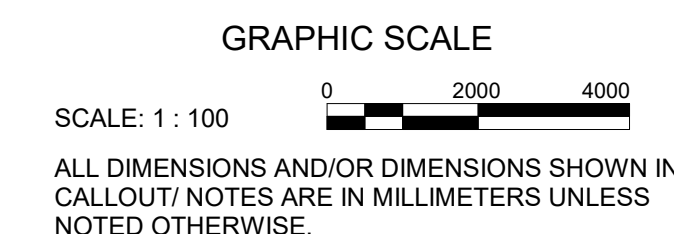

US Army Corps
of Engineers ®

MARK	DESCRIPTION	DATE


DESIGNED BY: E. YAO	ISSUE DATE: JUNE 2018	SOLICITATION NO.: W912AV-17-D-0003
DRAWN BY: R. TANGONAN	CHECKED BY: J. JUNG	CONTRACT NO.: W912AV-17-D-0003
SUBMITTED BY: J. JUNG	SIZE: ANSI D	US ARMY CORPS OF ENGINEERS JAPAN ENGINEER DISTRICT OKINAWA AREA OFFICE APO AP 96376-5132
SSAW INTERNATIONAL, INC. 507 SUMNER STREET, SUITE 620 HONOLULU, HAWAII 96817		

APO AP 96343-5010
FY20 MCA PN77833 VEHICLE MAINTENANCE SHOP
SSAW - EXTERIOR ELEVATIONS (CLIN 0004)


SHEET ID
SSAW
S-D201

INTERMEDIATE DESIGN


Plot Date: 12/16/2025 3:37:09 PM File Path: AutoCAD Docs \Vehicle Maint Shop Kadena\511756_1\TEMP_STRUC.dwg

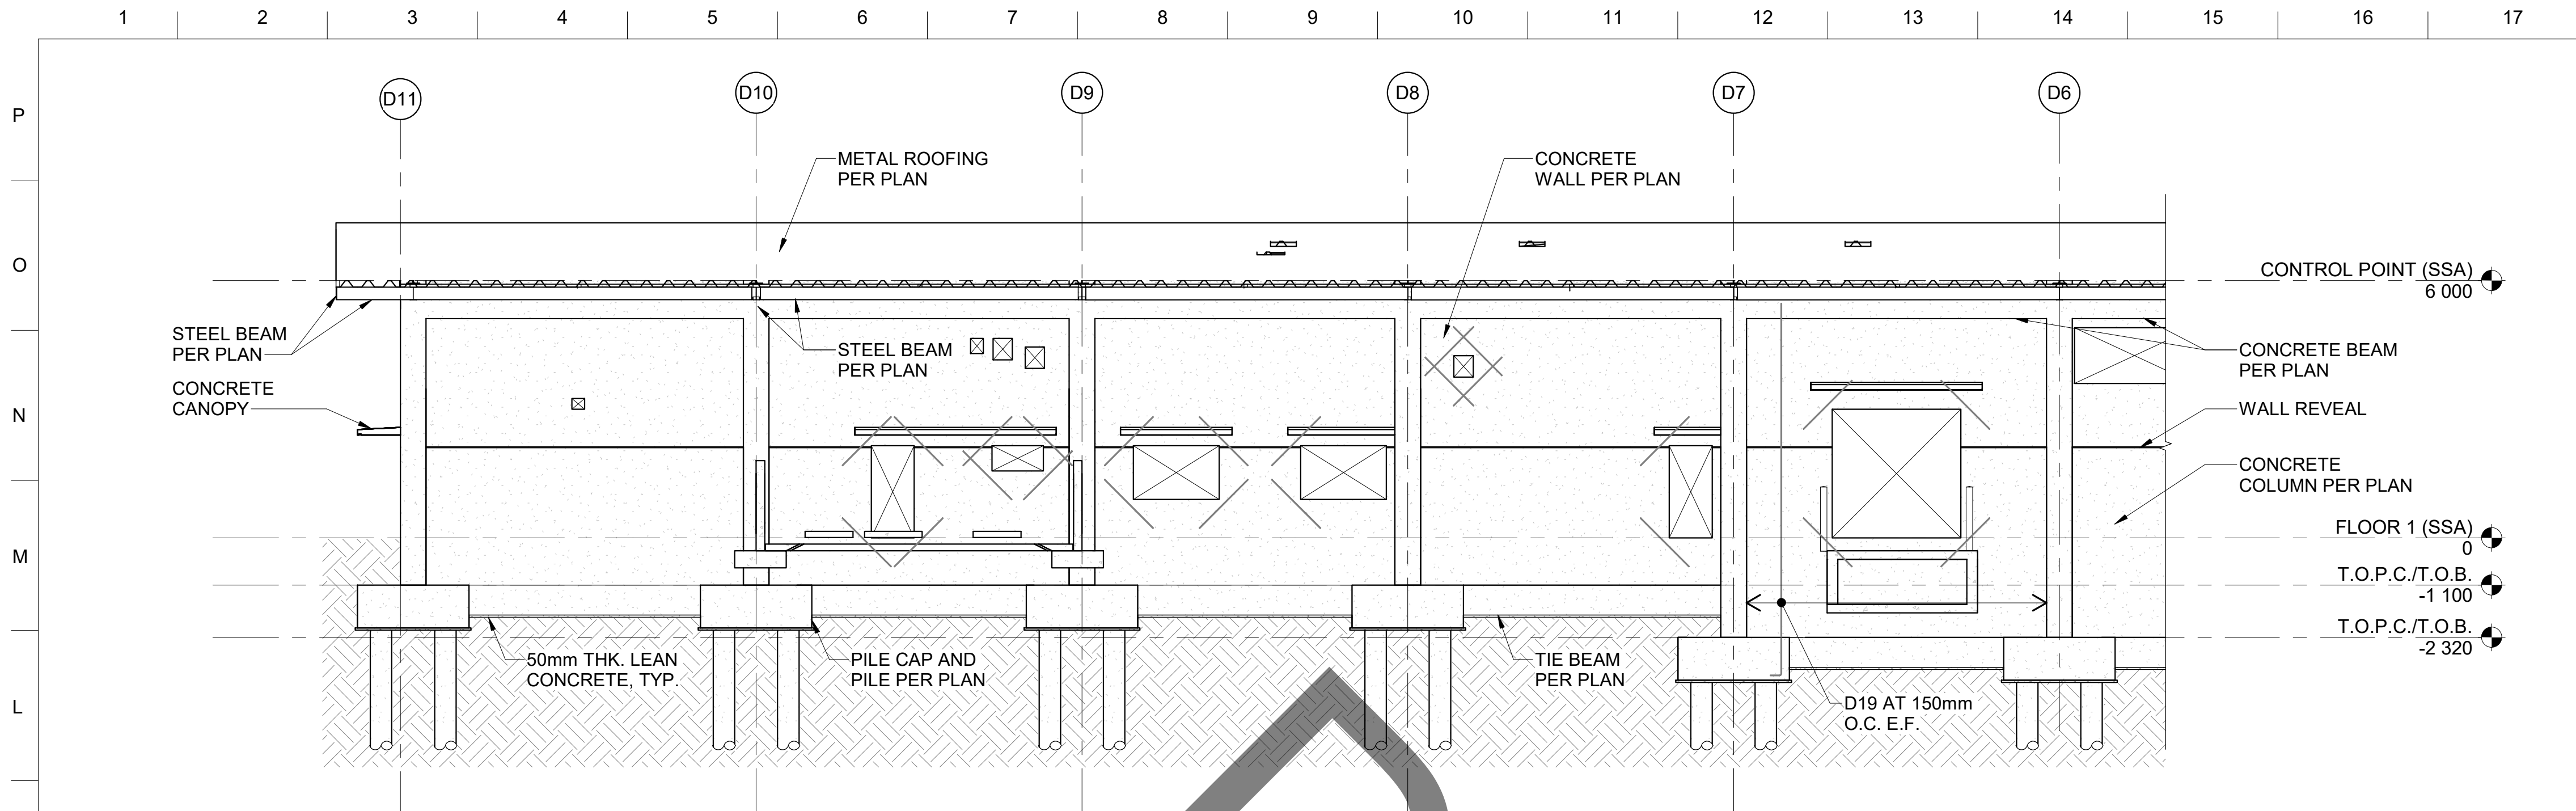

K1 SSAW - PARTIAL EXTERIOR ELEVATION - NORTH (EAST) (CLIN 004)
SCALE 1 : 100

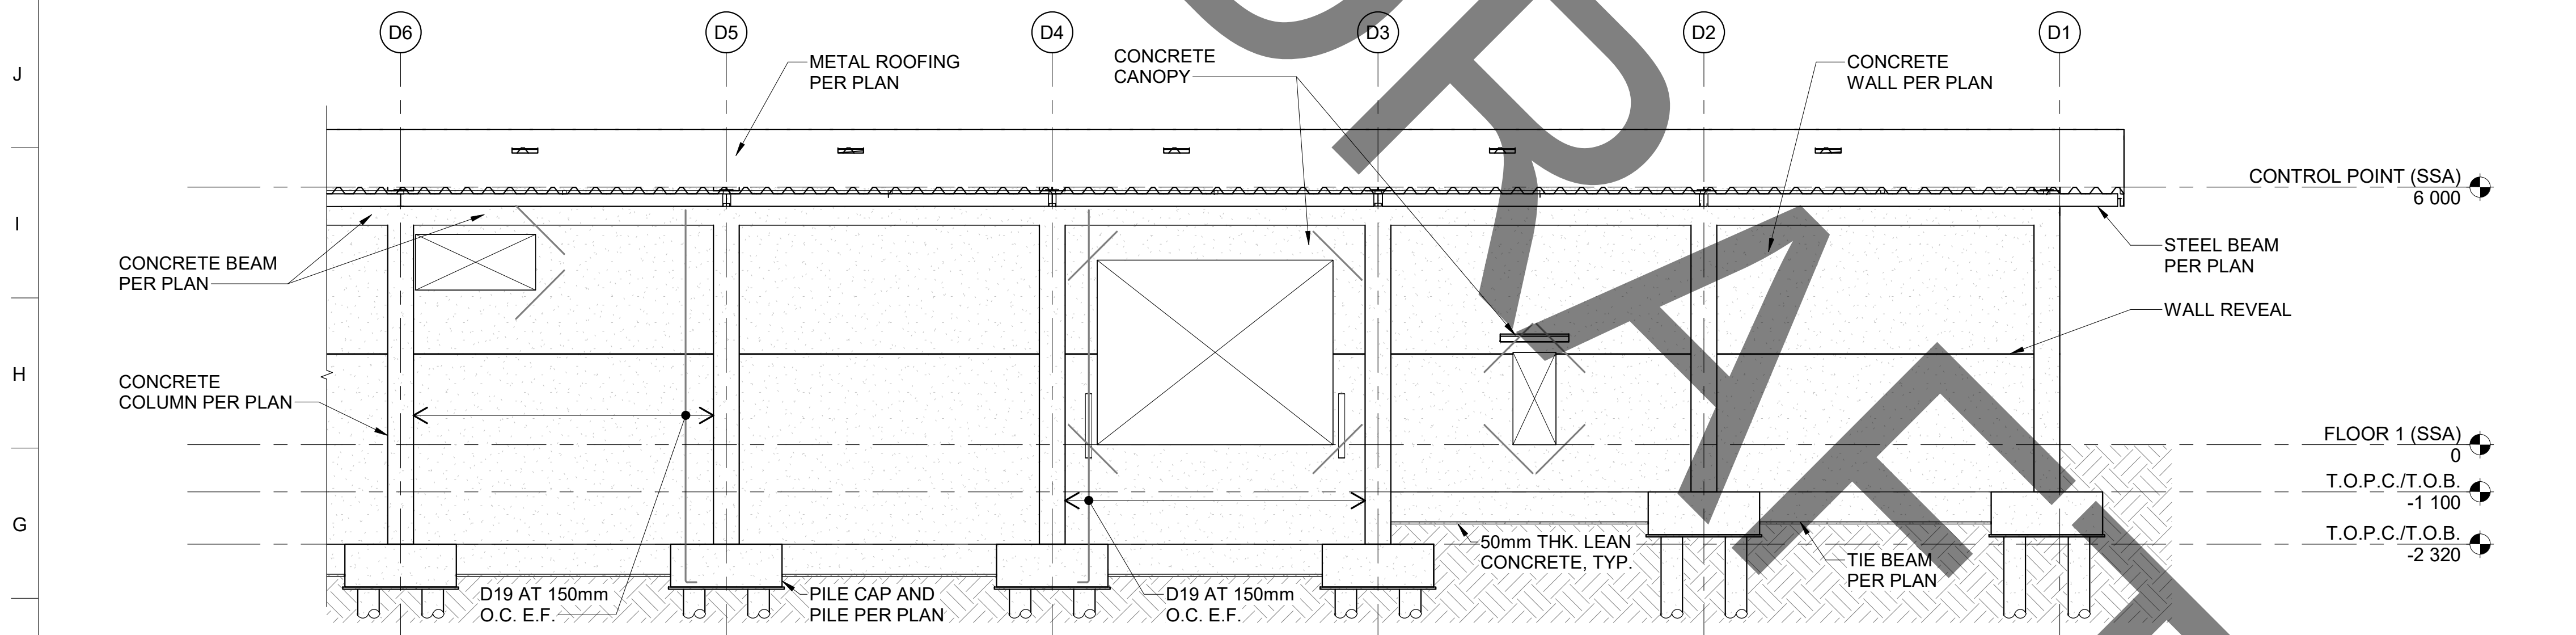

F1 SSAW - PARTIAL EXTERIOR ELEVATION - NORTH (WEST) (CLIN 004)
SCALE 1 : 100

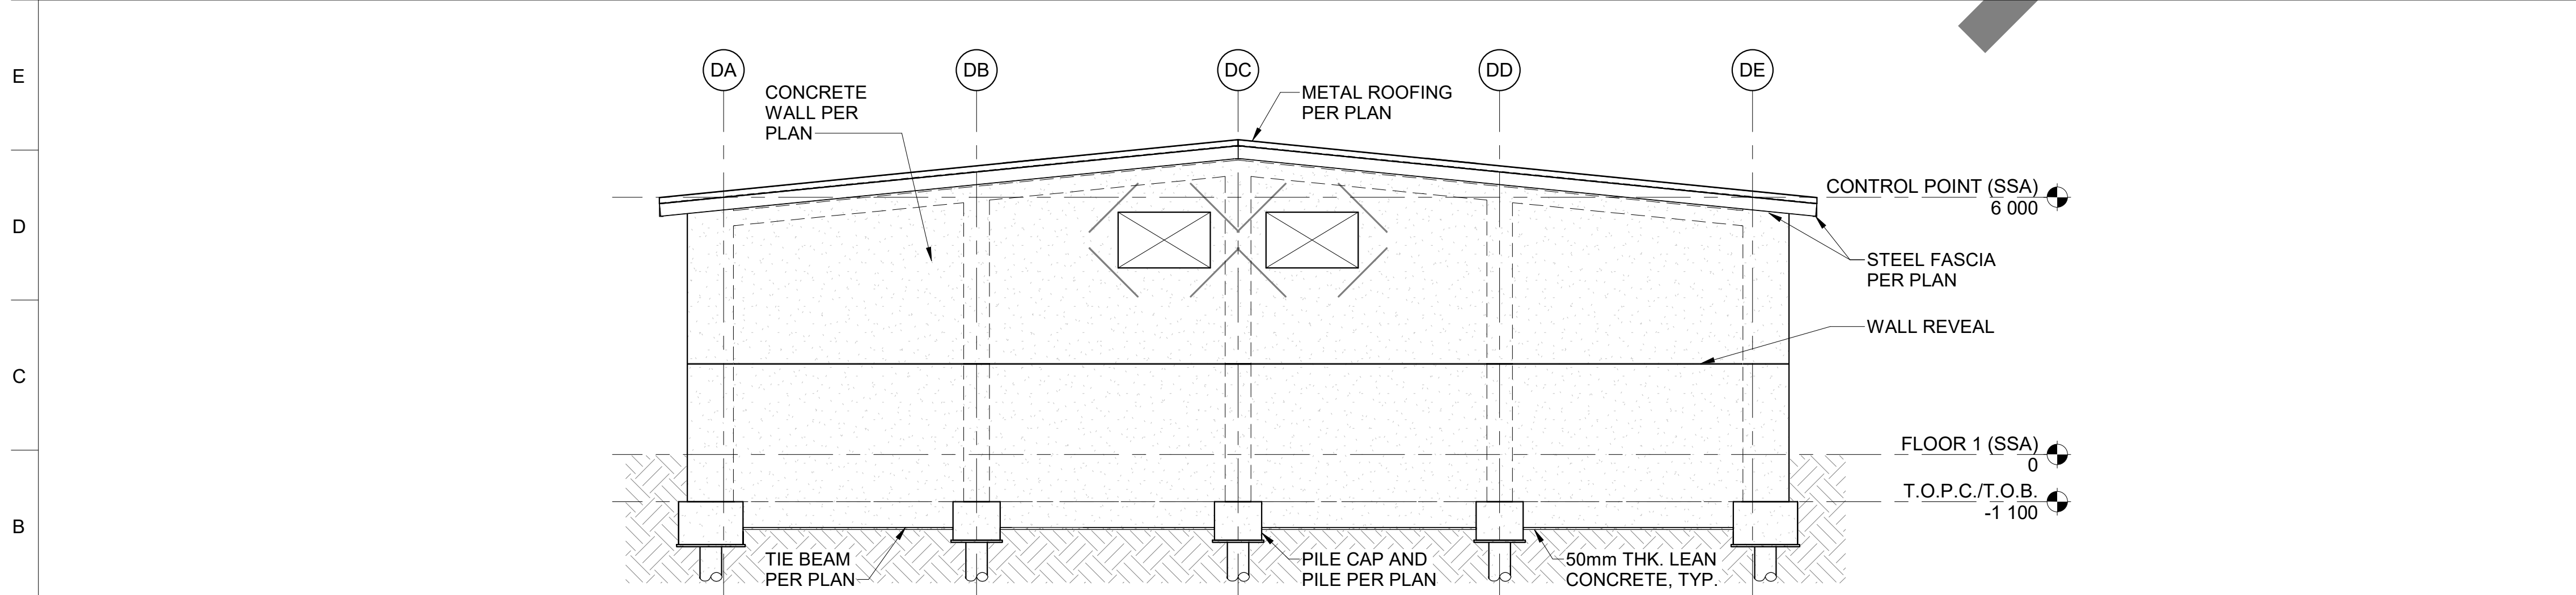

A1 SSAW - EXTERIOR ELEVATION - WEST (CLIN 0004)
SCALE 1 : 100

REFERENCE DRAWINGS


S-001 - GENERAL NOTES
S-002 - DESIGN DATA, DESIGN CODES AND STANDARDS, ABBREVIATION
S-501 - TYPICAL REINFORCING STEEL DETAILS
S-502 - TYPICAL CONCRETE DETAILS
S-601 - CONCRETE PILE CAP SCHEDULE
S-602 - CONCRETE PILE SCHEDULE
S-603 - CONCRETE GRADE BEAM AND TIE BEAM SCHEDULE
S-604 - CONCRETE FOOTING SCHEDULE
S-605 - CONCRETE WALL SCHEDULE
S-606 - CONCRETE COLUMN ELEVATION
S-607 - CONCRETE COLUMN SCHEDULE
S-608 - CONCRETE BEAM DETAIL
S-609 - CONCRETE BEAM SCHEDULE

NOTES

- SEE ARCHITECTURAL DRAWINGS FOR DIMENSIONS, ELEVATIONS AND DETAILS NOT SHOWN ON STRUCTURAL DRAWINGS.
- SEE ARCHITECTURAL DRAWINGS FOR FLOOR SLOPE.
- VERIFY WITH ARCHITECT/MECHANICAL FOR SIZE AND LOCATION OF OPENINGS.

CLIN 0004

GRAPHIC SCALE

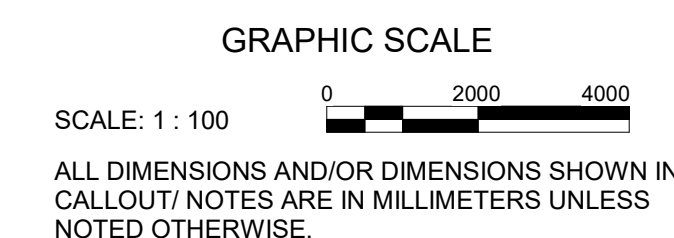

US Army Corps
of Engineers ®

DATE
DESCRIPTION
MARK

ISSUE DATE: JUNE 2018	SOLICITATION NO.: W72WY-17-D-0003
DESIGNED BY: E. YAO	CHECKED BY: J. UNO
DRAWN BY: R. TANGONAN	SUBMITTED BY: J. UNO
SIZE: ANSI D	

US ARMY CORPS OF ENGINEERS
JAPAN ENGINEER DISTRICT
OKINAWA AREA OFFICE
APO AP 96376-5132



SSAW
STRUCTURAL INC.
507 SUMNER STREET, SUITE 620
HONOLULU, HAWAII 96817

APO AP 96343-5010
FY20 MCA PN77833 VEHICLE MAINTENANCE SHOP
SSAW - EXTERIOR ELEVATIONS (CLIN 0004)


SHEET ID
SSAW
S-D202

INTERMEDIATE DESIGN

Plot Date: 12/16/2025 3:37:12 PM File Path: Autocad Docs \Vehicle Maint Shop Kadena\5117561.TEMF.STRUC.plt

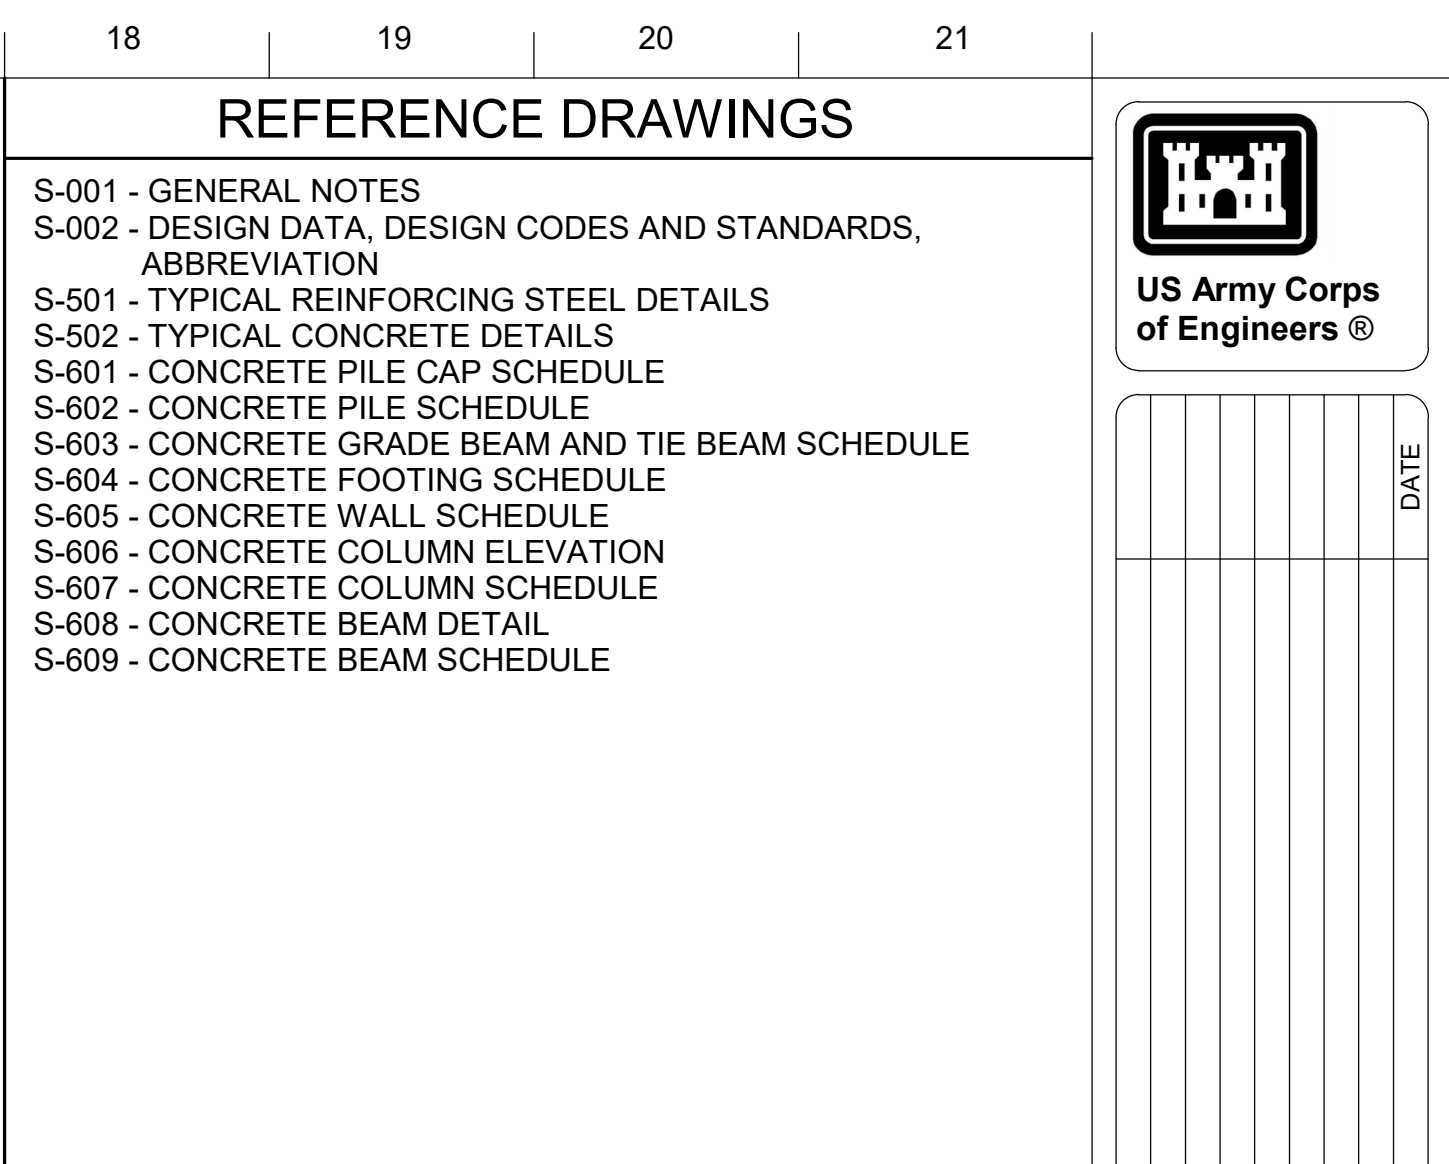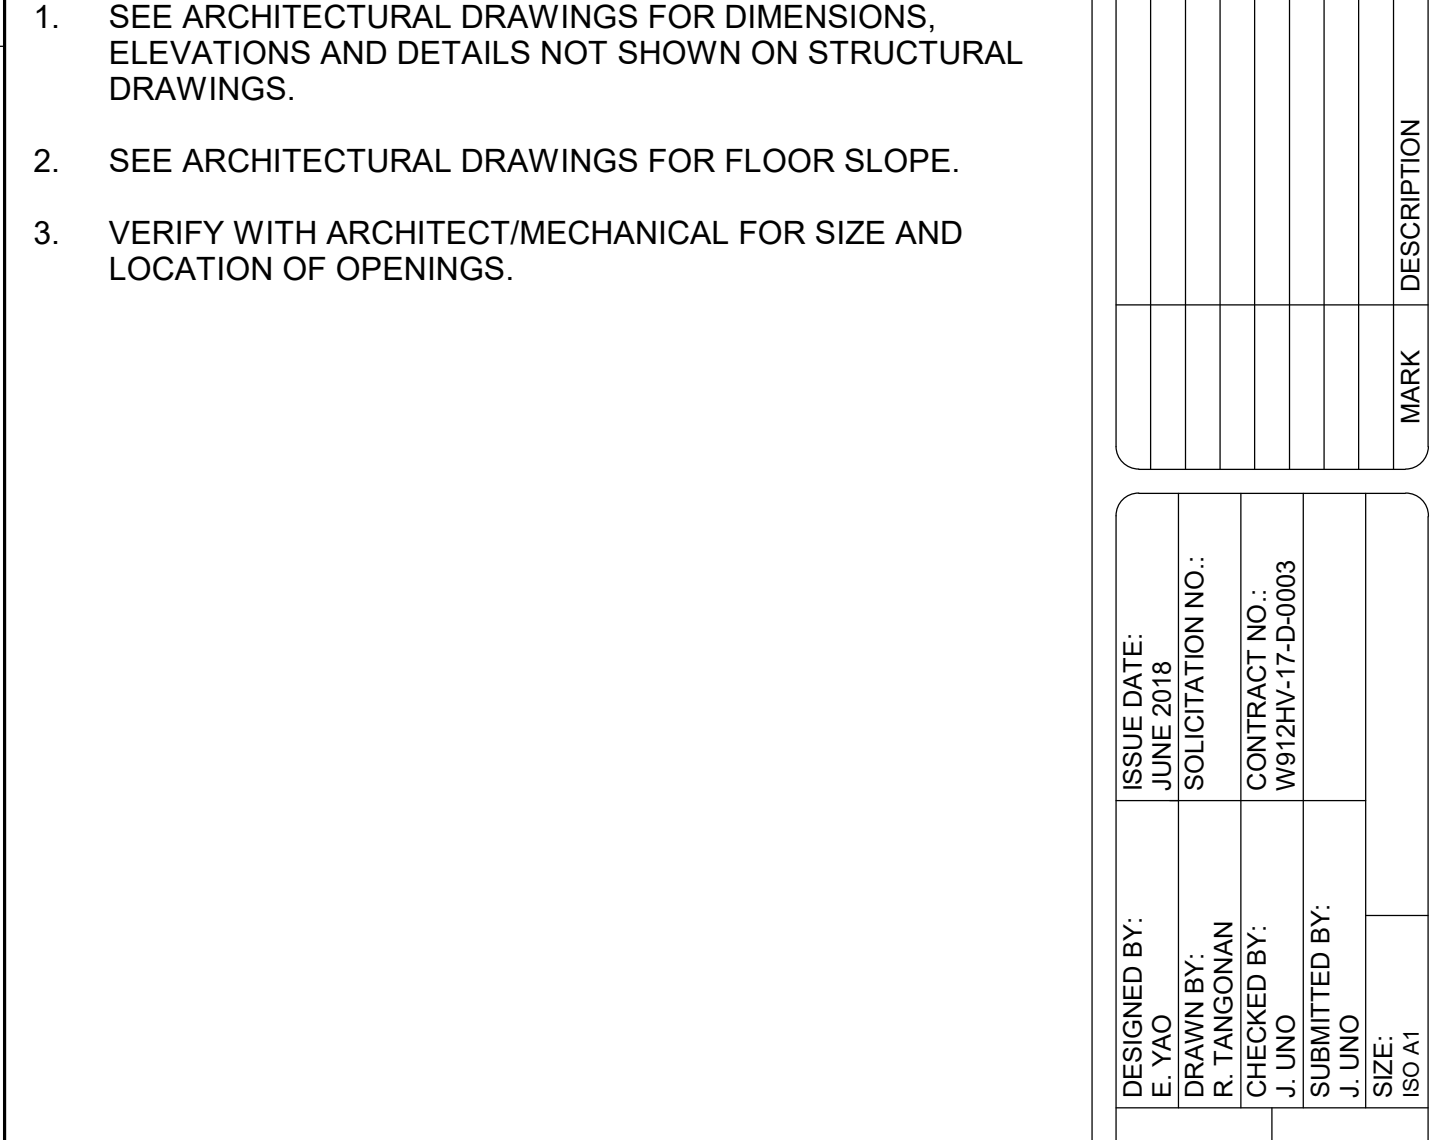[illegible]

ENGINEERS AREA OFFICE
2
2
2
1
INC
TE 620
817

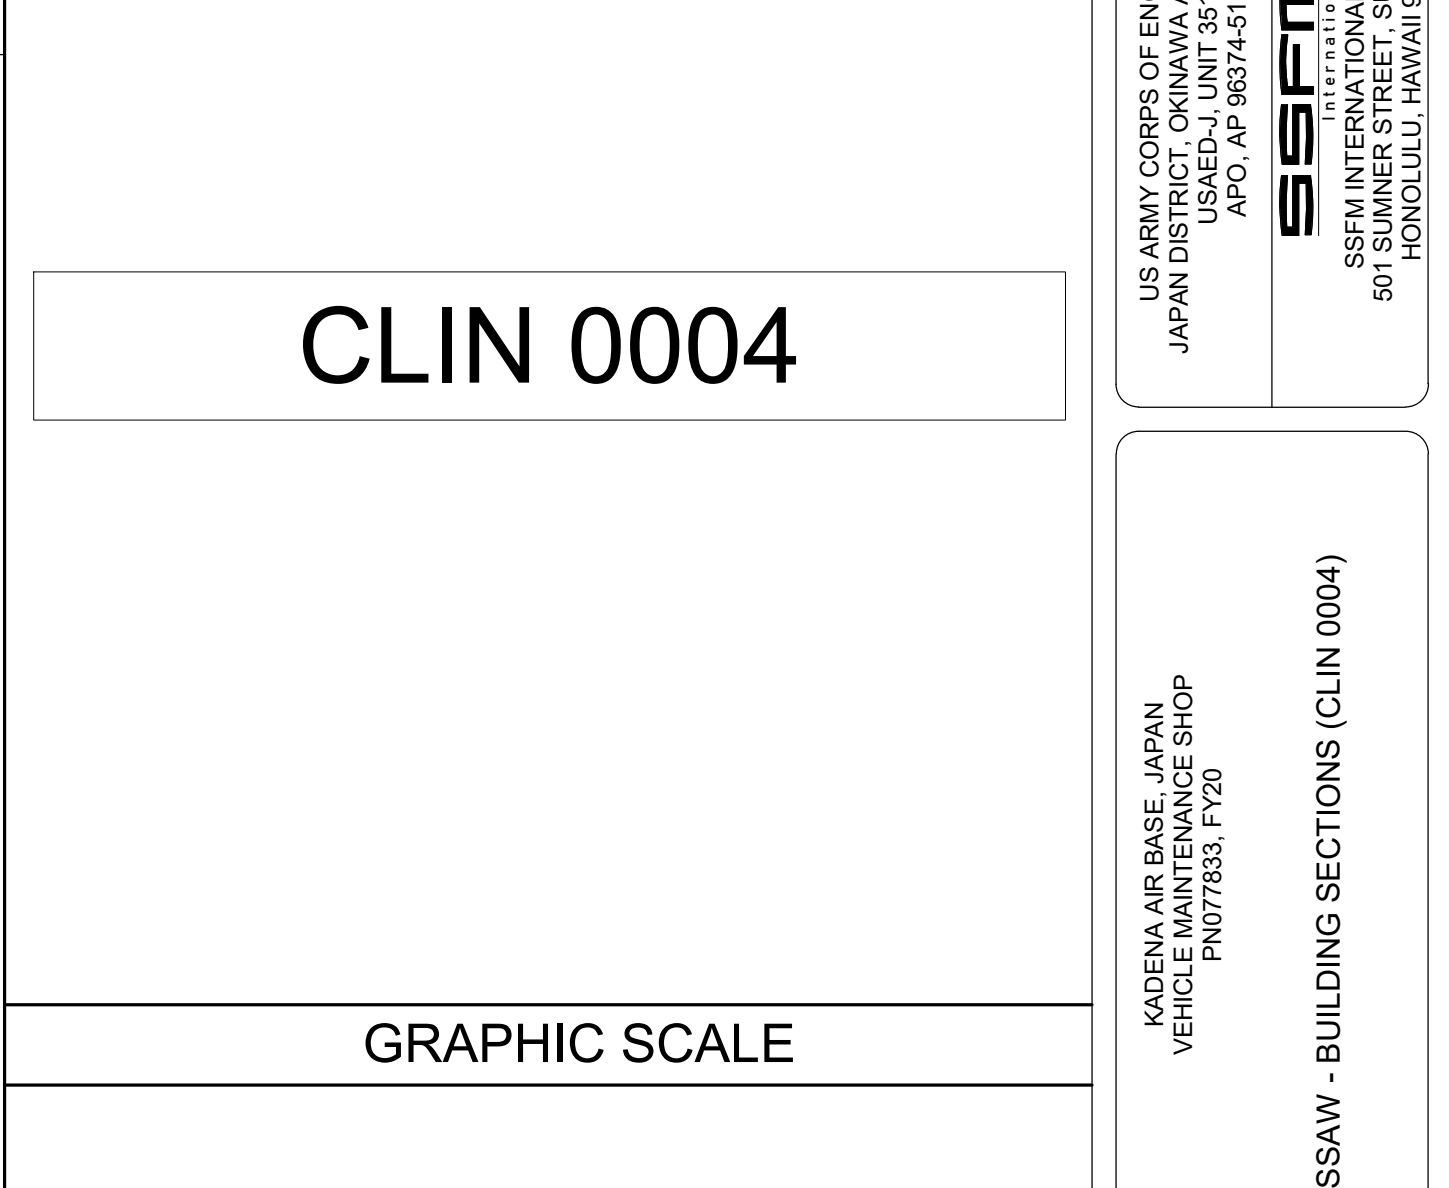

SCALE: 1 : 100

ALL DIMENSIONS AND/OR DIMENSIONS SHOWN IN
CALLOUT/ NOTES ARE IN MILLIMETERS UNLESS
NOTED OTHERWISE

SSAW
S-D301

MARK	DESCRIPTION
------	-------------

[illegible]

1. SEE ARCHITECTURAL DRAWINGS FOR DIMENSIONS, ELEVATIONS AND DETAILS NOT SHOWN ON STRUCTURAL DRAWINGS.
2. SEE ARCHITECTURAL DRAWINGS FOR FLOOR SLOPE.
3. VERIFY WITH ARCHITECT/MECHANICAL FOR SIZE AND LOCATION OF OPENINGS.

US ARMY CORPS OF ENGINEERS
 JAPAN ENGINEER DISTRICT
 KINAWA AREA OFFICE
 APO AP 96376-5132

ISSUED DATE:
 JUNE 2018
 SOLICITATION NO.:
 CONTRACT NO.:
 W912HV-17-D-0003

DESIGNED BY:
 E. YAO
 R. TANGONAN
 CHECKED BY:
 J. UNO
 SUBMITTED BY:
 J. UNO


SSM
 INTERNATIONAL, INC
 500 KALANIANAʻOHE BLVD
 HONOLULU, HAWAII 96817

Plot Date:	12/16/2025 3:37:14 PM	File Path:
------------	-----------------------	------------

SSAW - BUILDING SECTIONS (CLIN 0004

SHEET ID
SSAW
-D302

INTERMEDIATE DESIGN

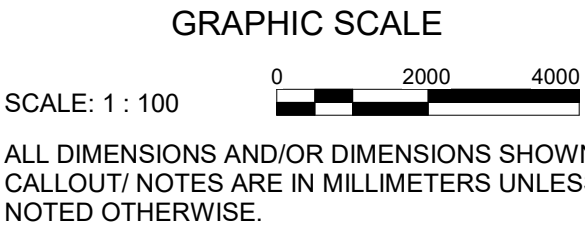

A1

SSAW - BUILDING SECTION (CLIN 004)

SCALE 1 : 100




GRAPHIC SCALE

SCALE: 1 : 20



ALL DIMENSIONS AND/OR DIMENSIONS SHOWN IN
CALLOUT/ NOTES ARE IN MILLIMETERS UNLESS
NOTED OTHERWISE.

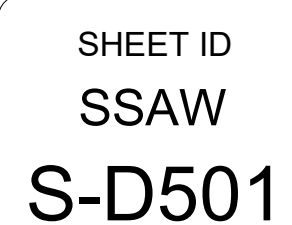

[illegible]

US ARMY CORPS OF ENGINEERS JAPAN ENGINEER DISTRICT OKINAWA AREA OFFICE APO AF 96376-5132	DESIGNED BY: DRAWN BY: R. TANGONAN CHECKED BY: J. LUNO SUBMITTED BY: J. LUNO SIZE:	ISSUE DATE: JUNE 2018 SOLICITATION NO.: CONTRACT NO.: W912HW-17-D-0003
---	---	--


APO AP 96343-5010
FY20 MCA PN77833 VEHICLE MAINTENANCE SHOP
SSAW - SECTIONS AND DETAILS (CLIN 0004)

SHEET ID
SSAW
S-D502

File Path: AutodesK Docs:\Vehicle Maint Shop Kadena\511758 TEMF STRUC.vt


Plot Date: 12/16/2025 3:37:16 PM

INTERMEDIATE DESIGN

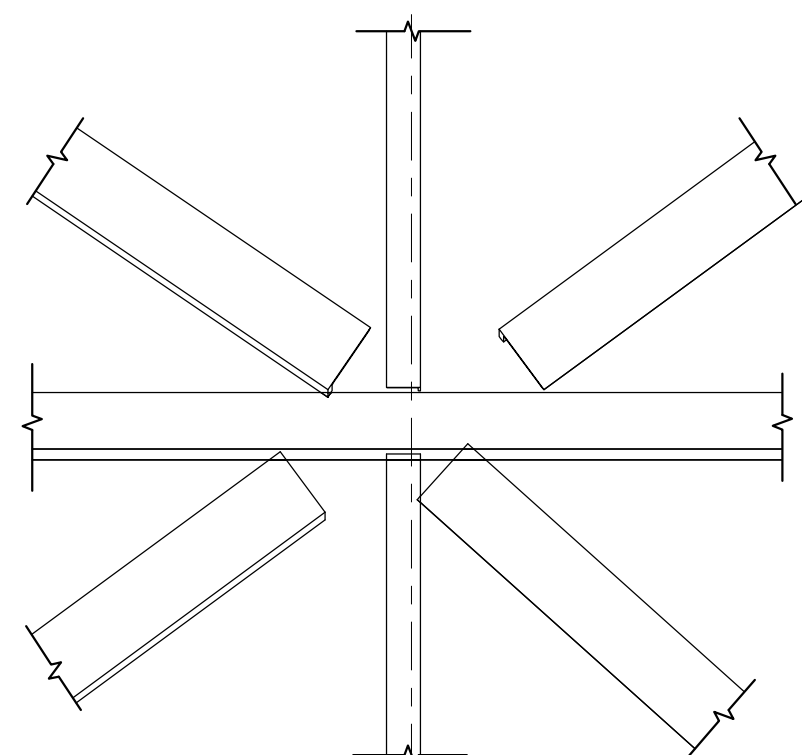


L1 SECTION
SCALE 1 : 20

SCALE 1 : 20

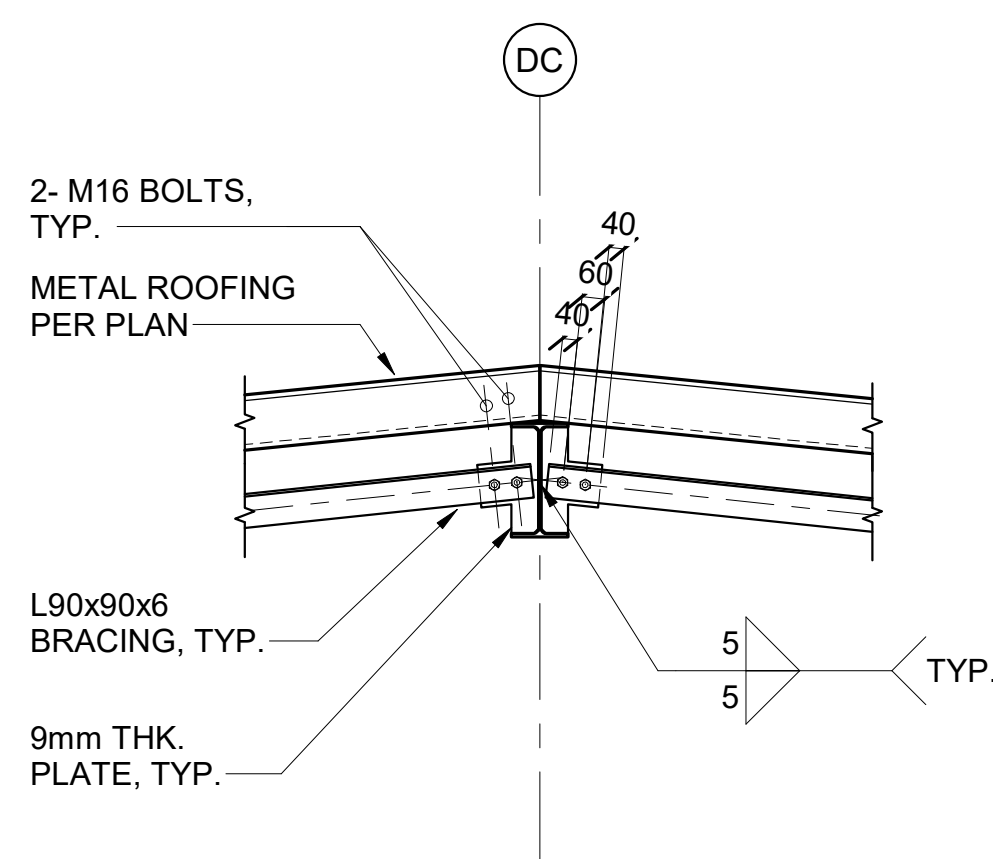

A17 SECTION


SCALE 1 : 20

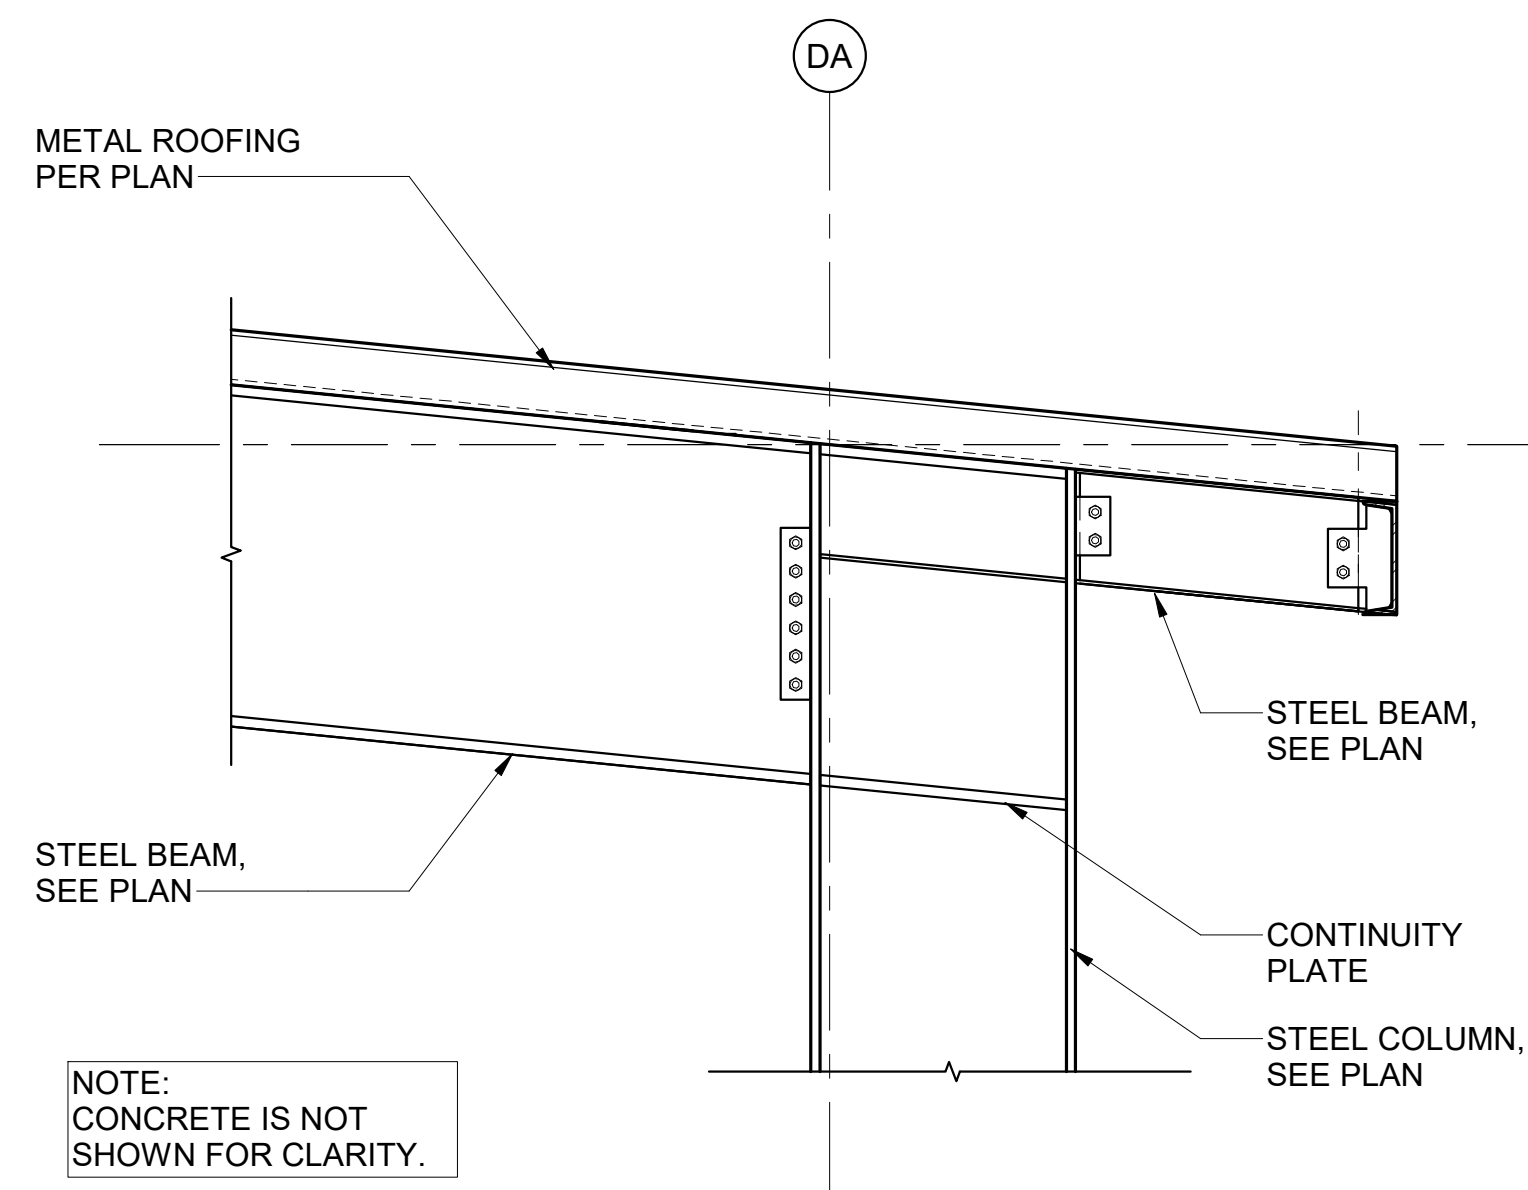

NOTE:
CONCRETE IS NOT
SHOWN FOR CLARITY.

A1 SECTION
SCALE 1 : 20

SCALE 1 : 20

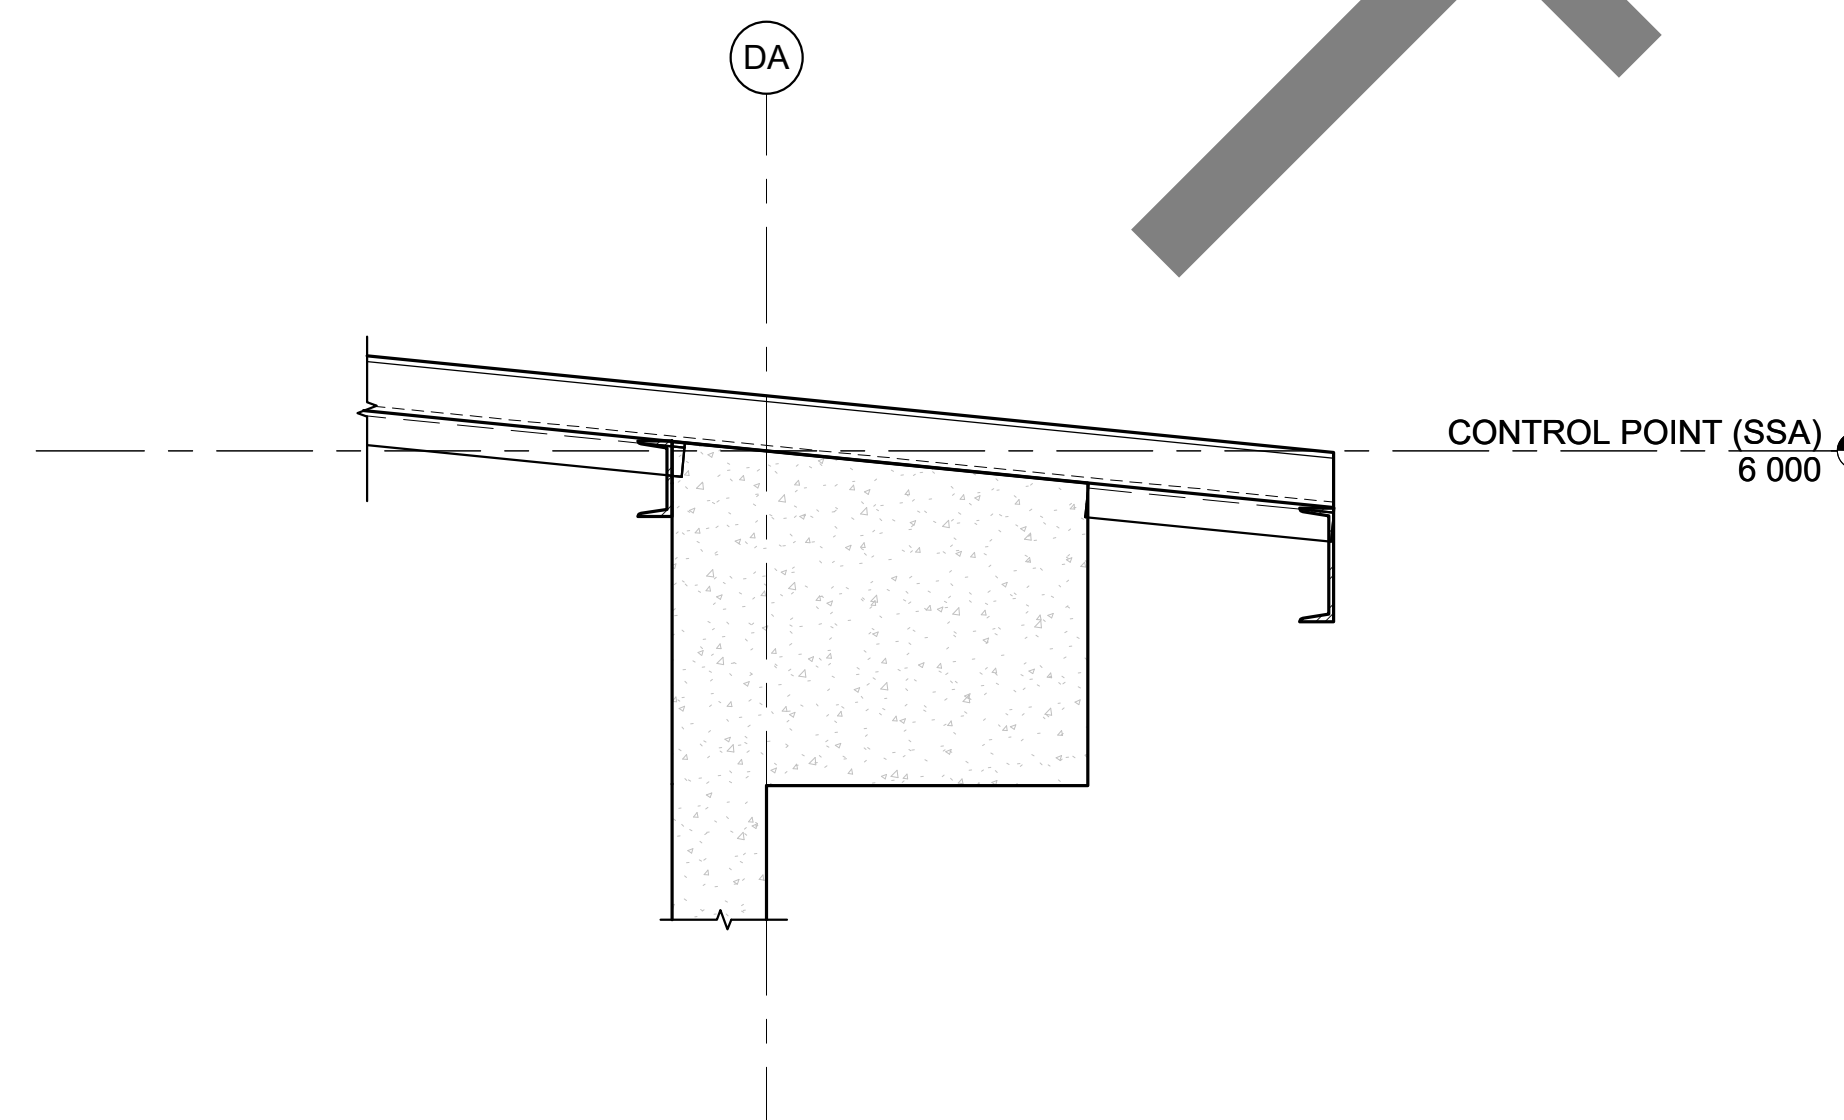


SECTION

SCALE 1 : 20

CLIN 0004

GRAPHIC SCALE

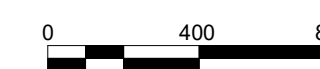

SCALE: 1 : 20

ALL DIMENSIONS AND/OR DIMENSIONS SHOWN IN
CALLOUT/ NOTES ARE IN MILLIMETERS UNLESS
NOTED OTHERWISE.



GRAPHIC SCALE

CLIN 0004

[illegible]




SSAW - SECTIONS AND DETAILS (CLIN 0004)

INTERMEDIATE DESIGN

Plot Date: 12/16/2025 3:37:17 PM File Path: Autodesk Docs://Vehicle Maint Shop Kadena/511758_TEMF_STRUCT.M

File Path:

Plot Date: 12/16/2025 3:37:17 PM

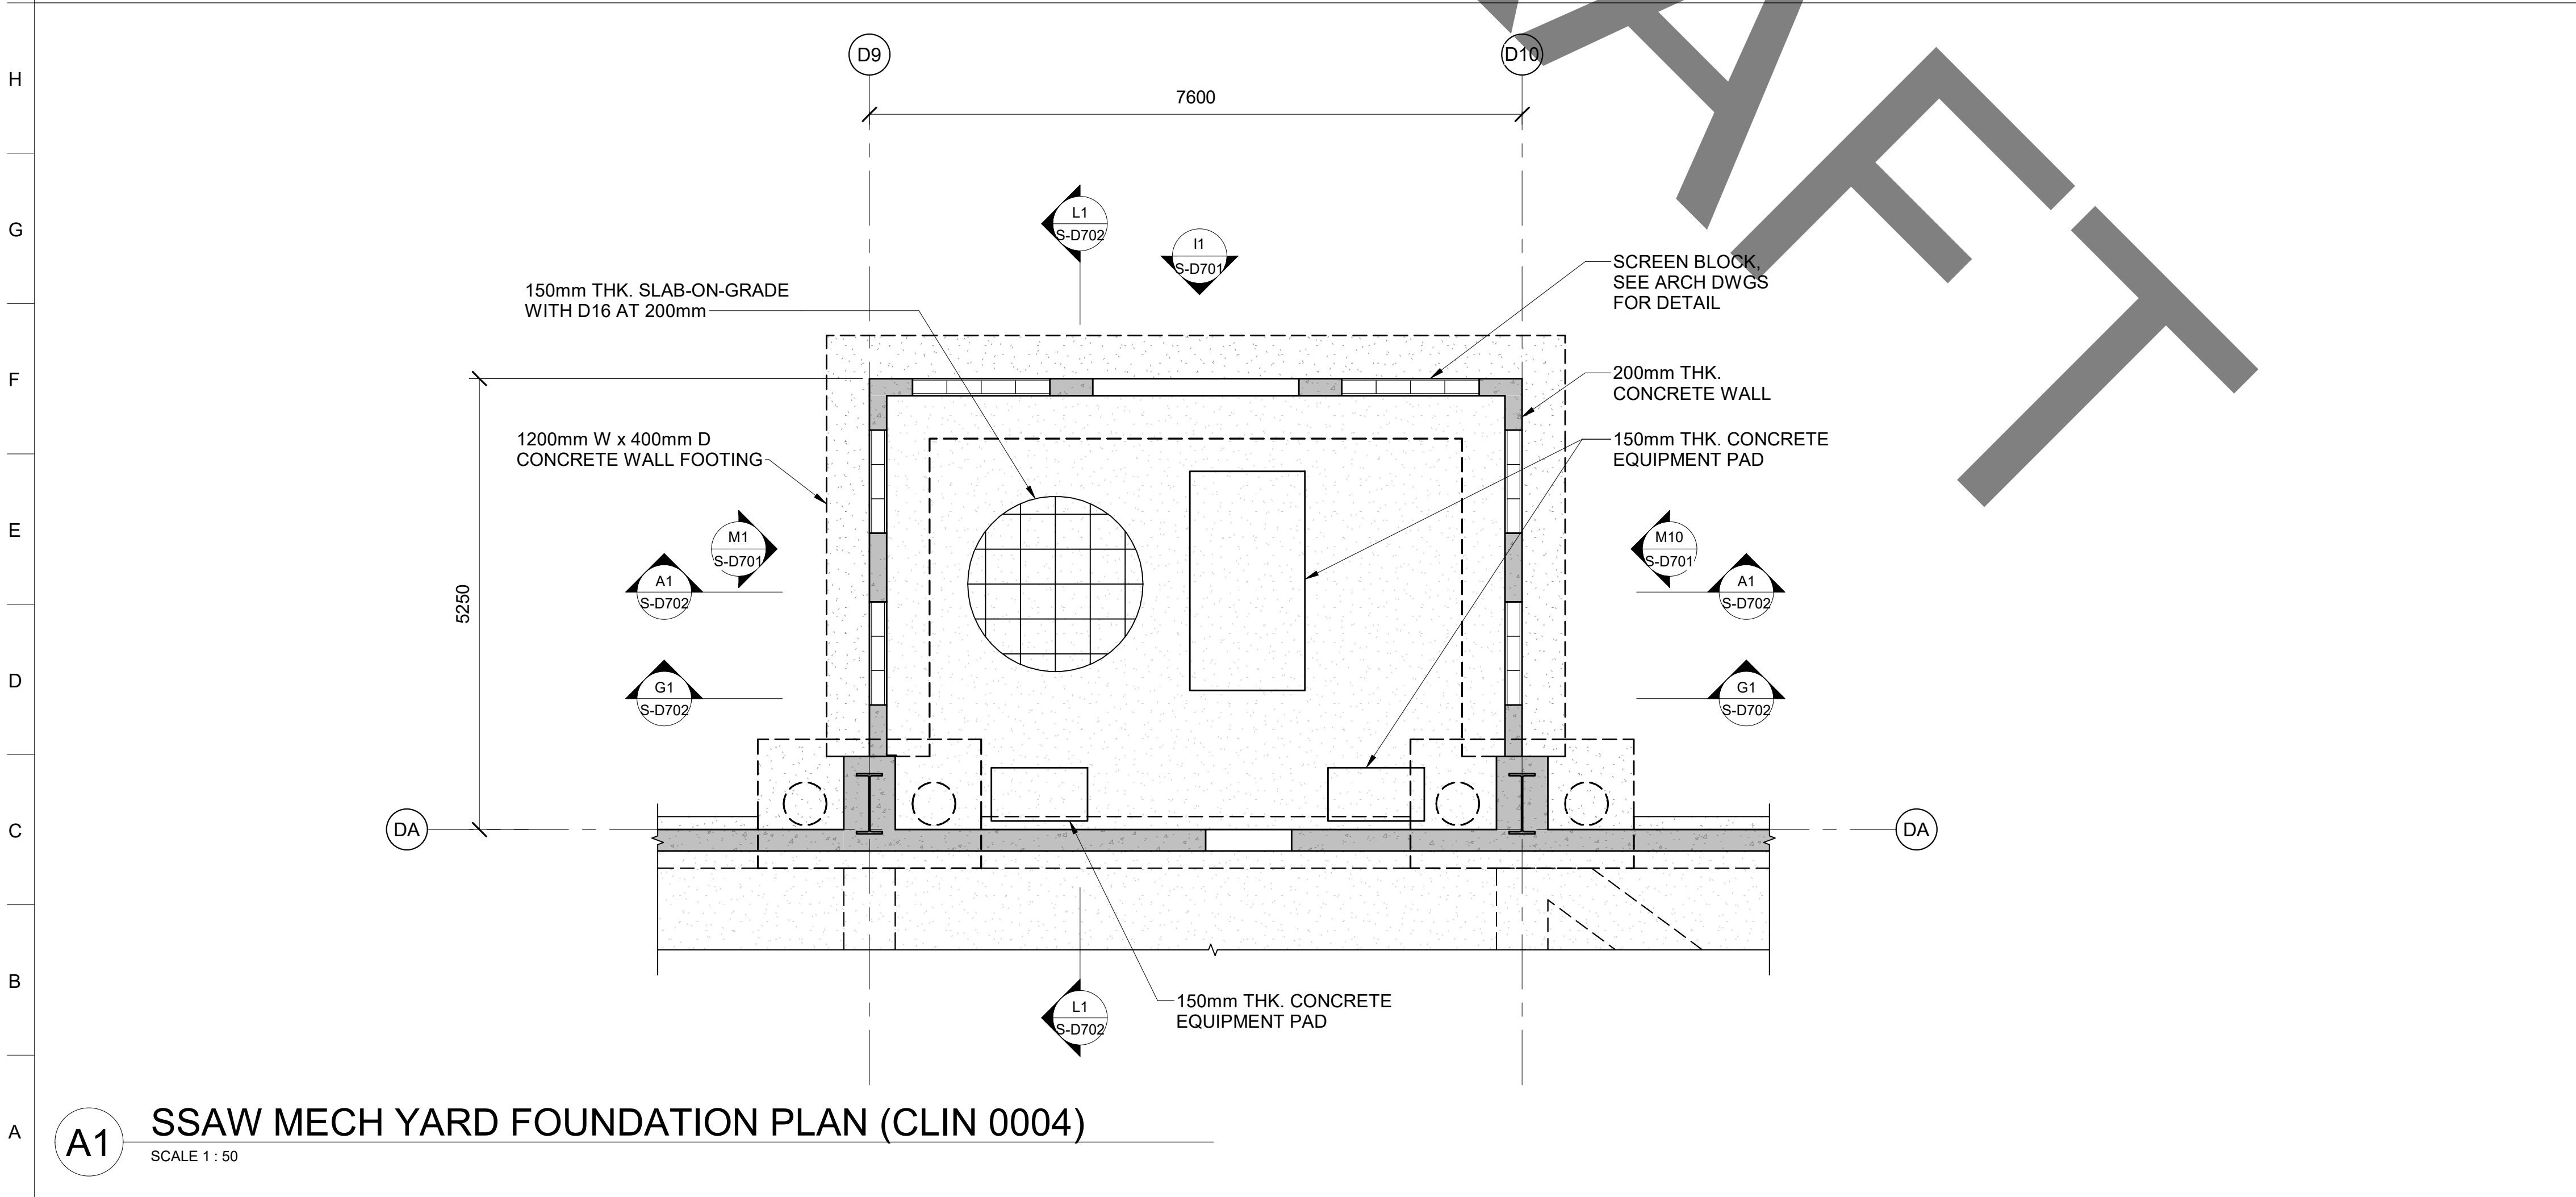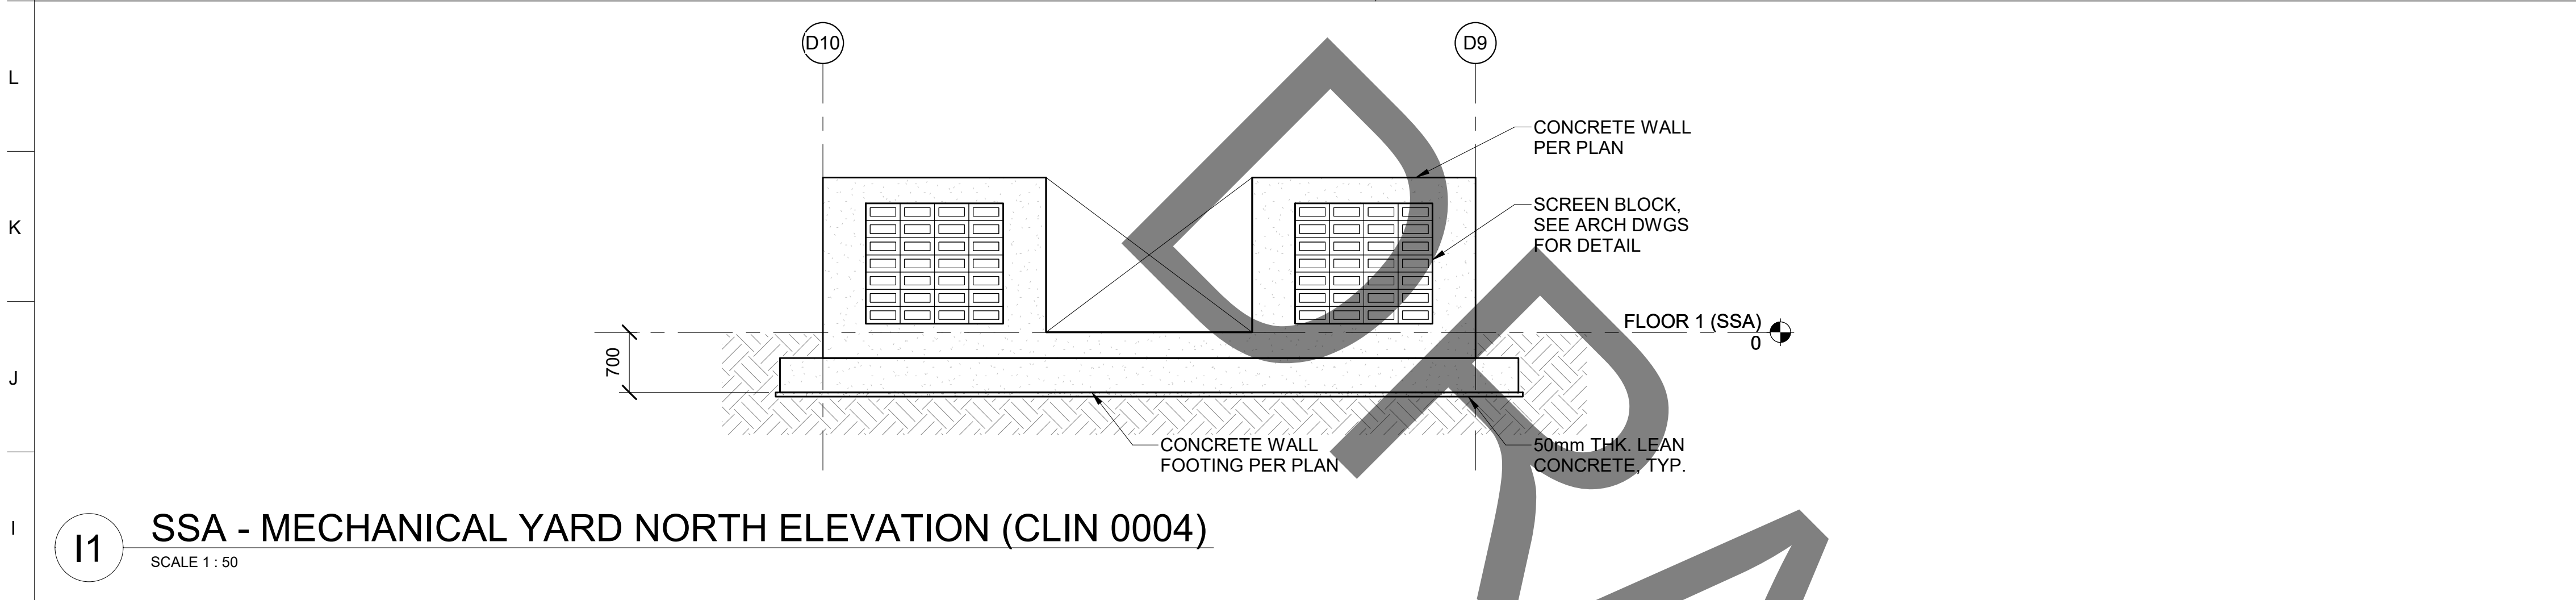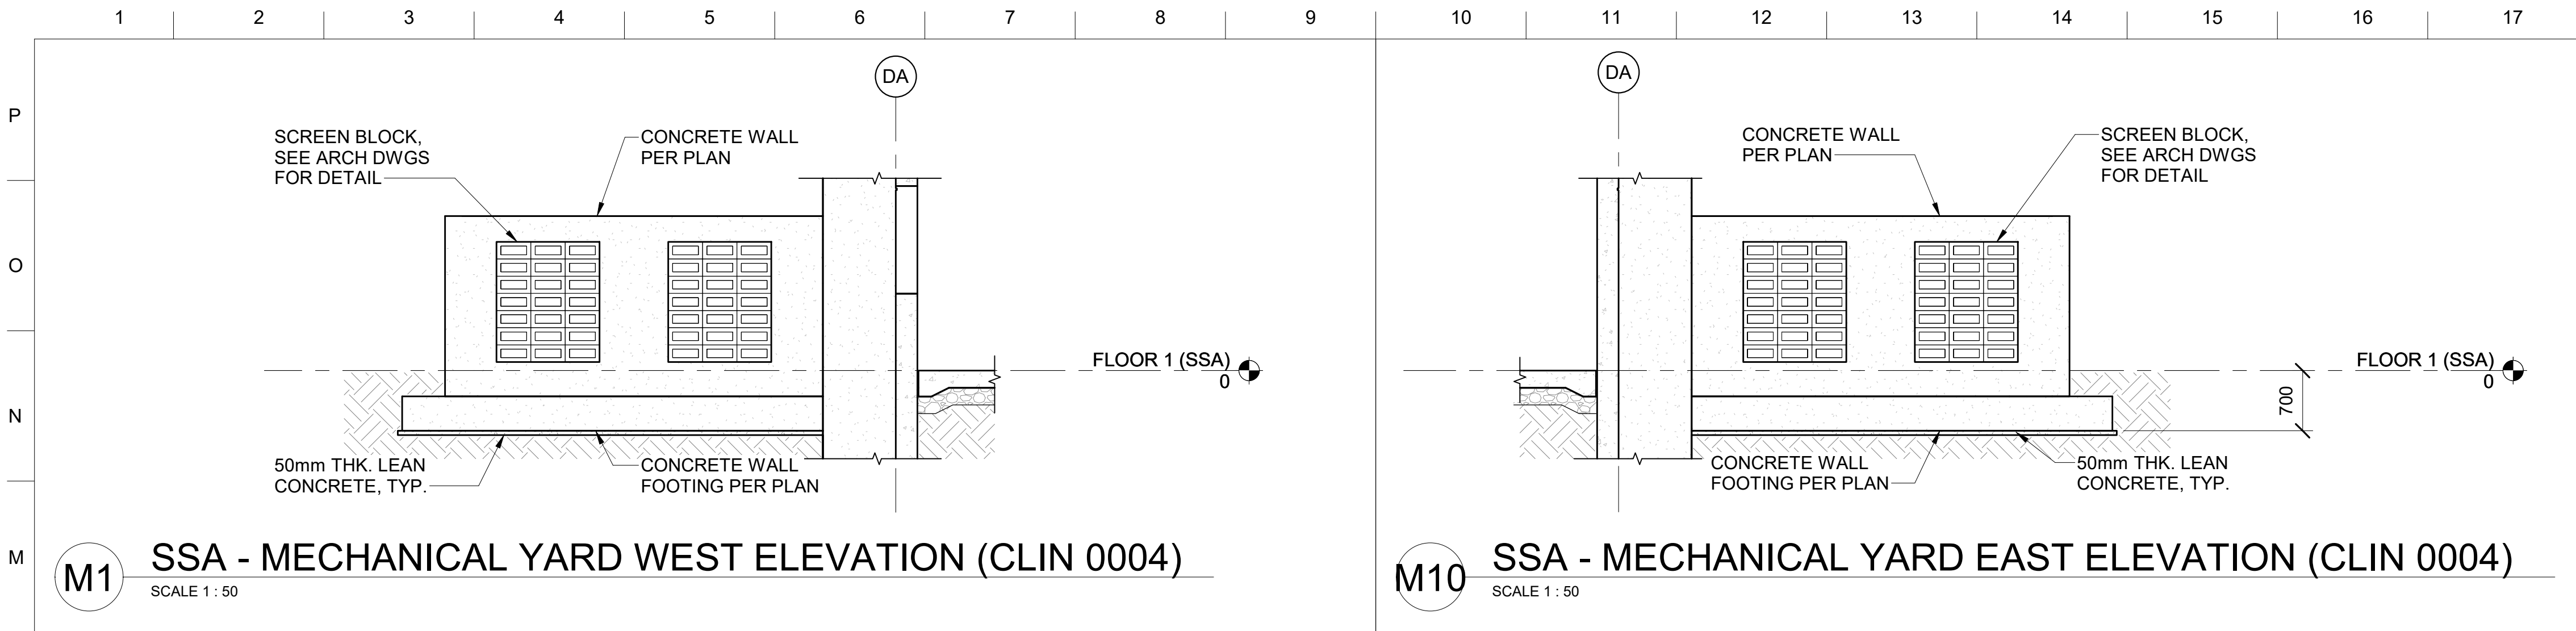

18 19 20 21

REFERENCE DRAWINGS

S-001 - GENERAL NOTES
S-002 - DESIGN DATA, DESIGN CODES AND STANDARDS, ABBREVIATION
S-501 - TYPICAL REINFORCING STEEL DETAILS
S-502 - TYPICAL CONCRETE DETAILS
S-604 - CONCRETE FOOTING SCHEDULE
S-605 - CONCRETE WALL SCHEDULE

DATE

MARK

DESCRIPTION

NOTES

- SEE ARCHITECTURAL DRAWINGS FOR DIMENSIONS, ELEVATIONS AND DETAILS NOT SHOWN ON STRUCTURAL DRAWINGS.
- SEE ARCHITECTURAL DRAWINGS FOR FLOOR SLOPE.
- VERIFY WITH ARCHITECT/MECHANICAL FOR SIZE AND LOCATION OF OPENINGS.
- THICKNESS OF CONCRETE SLABS SHOWN ARE MINIMUM AND MUST BE MAINTAINED AT SLOPED PORTION.
- SEE CIVIL DRAWINGS FOR FINISH FLOOR ELEVATION.
- TYP TOP OF SLAB-ONGRADE EL = 0 UNO
- TYP TOP OF FOOTING EL = -600 UNO

DESIGNED BY: E. YAO
DRAWN BY: R. TANGONAN
CHECKED BY: J. UNO
SUBMITTED BY: J. UNO
SIZE: ANSI D

ISSUE DATE: JUNE 2018
SOLICITATION NO.:
CONTRACT NO.: W912AV-17-D-0003

US ARMY CORPS OF ENGINEERS
JAPAN ENGINEER DISTRICT
OKINAWA AREA OFFICE
APO AP 96376-5132

SSFM
SSFM INTERNATIONAL INC.
501 SUMNER STREET, SUITE 620
HONOLULU, HAWAII 96817

CLIN 0004

GRAPHIC SCALE

GRAPHIC SCALE
SCALE: 1 : 50
0 1000 2000

ALL DIMENSIONS AND/OR DIMENSIONS SHOWN IN CALLOUT/ NOTES ARE IN MILLIMETERS UNLESS NOTED OTHERWISE.

APO AP 96343-5010
FY20 MCA PN7833 VEHICLE MAINTENANCE SHOP

**SSAW - MECHANICAL YARD FOUNDATION PLAN
ANF ELEVATIONS (CLIN 0004)**

SHEET ID
**SSAW
S-D701**



**US Army Corps
of Engineers ®**


Autodesk Docs / Vehicle Maint Shop Kadena51736 / TEMP STRUCT.rvt

File Path: 12/16/2025 3:37:19 PM


Plot Date:

INTERMEDIATE DESIGN

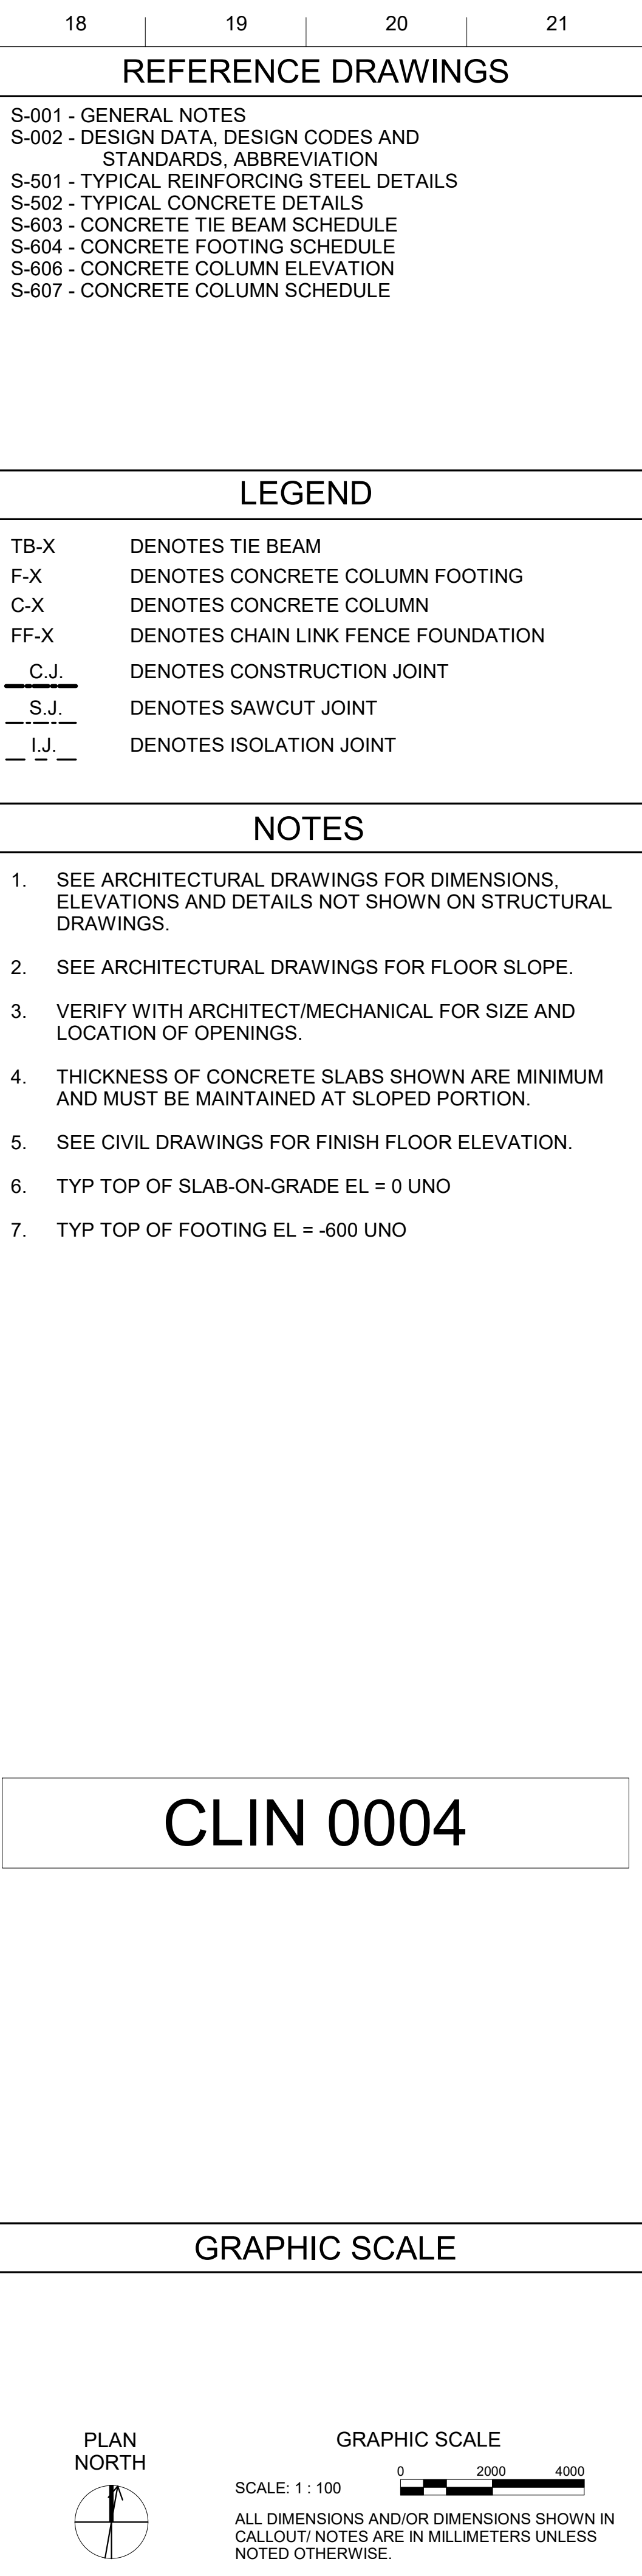[illegible]

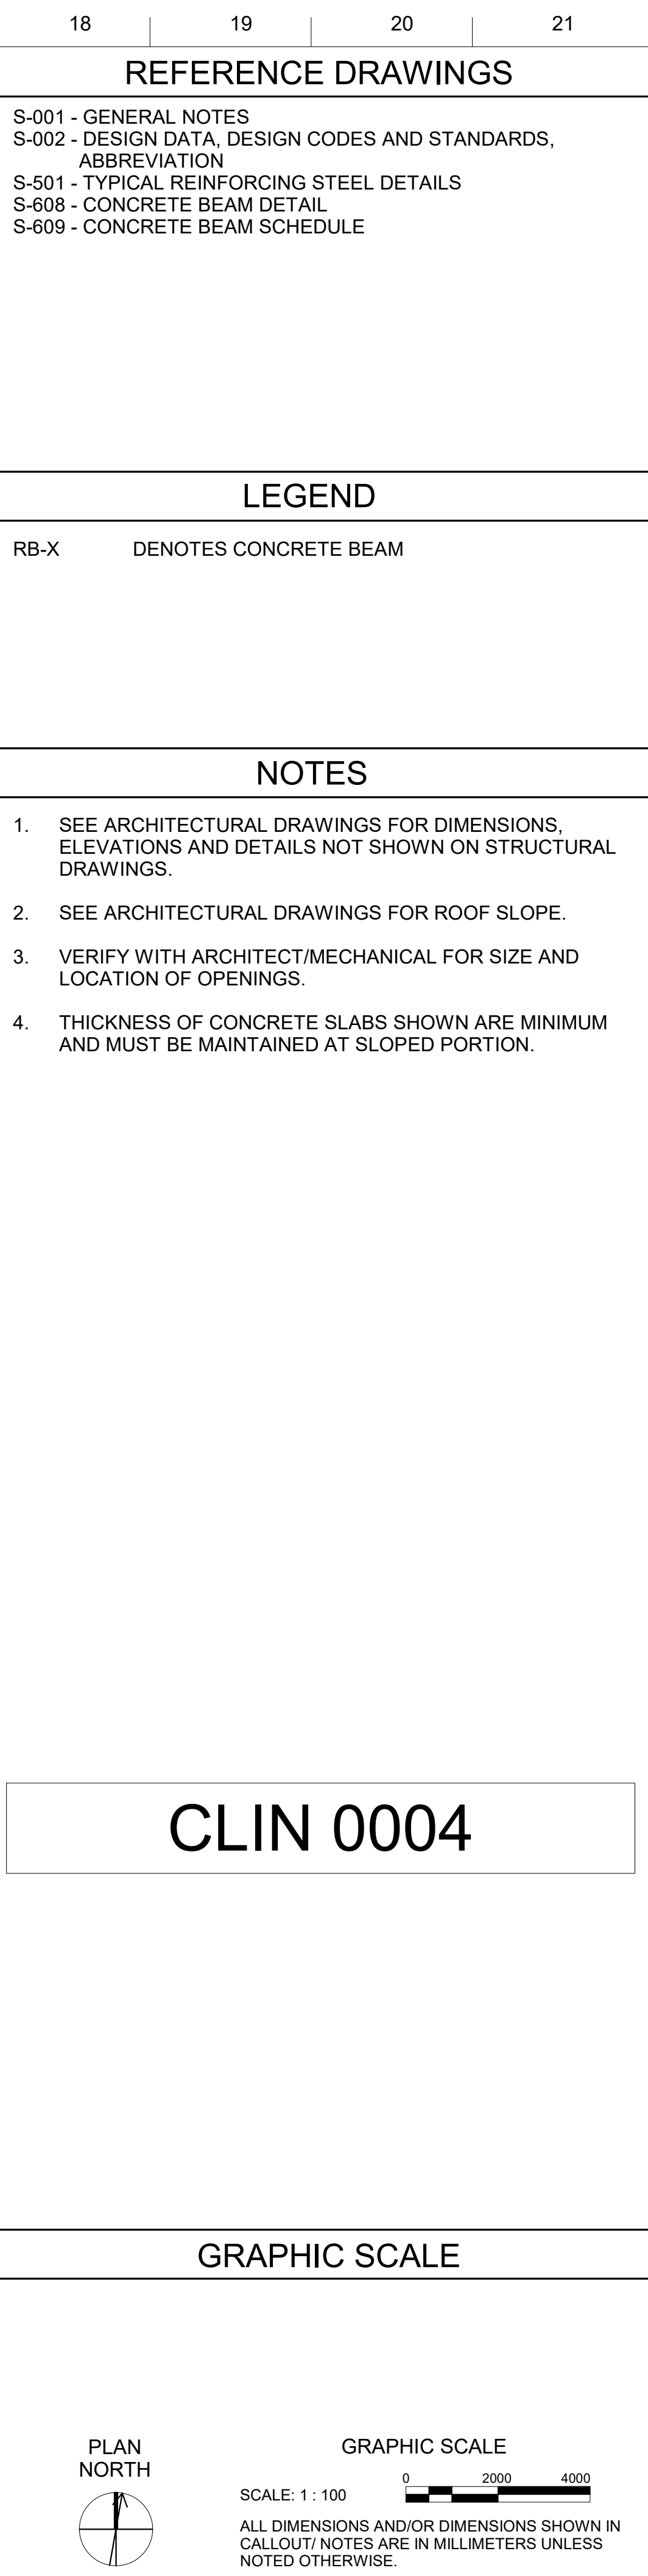[illegible]

INTERMEDIATE DESIGN

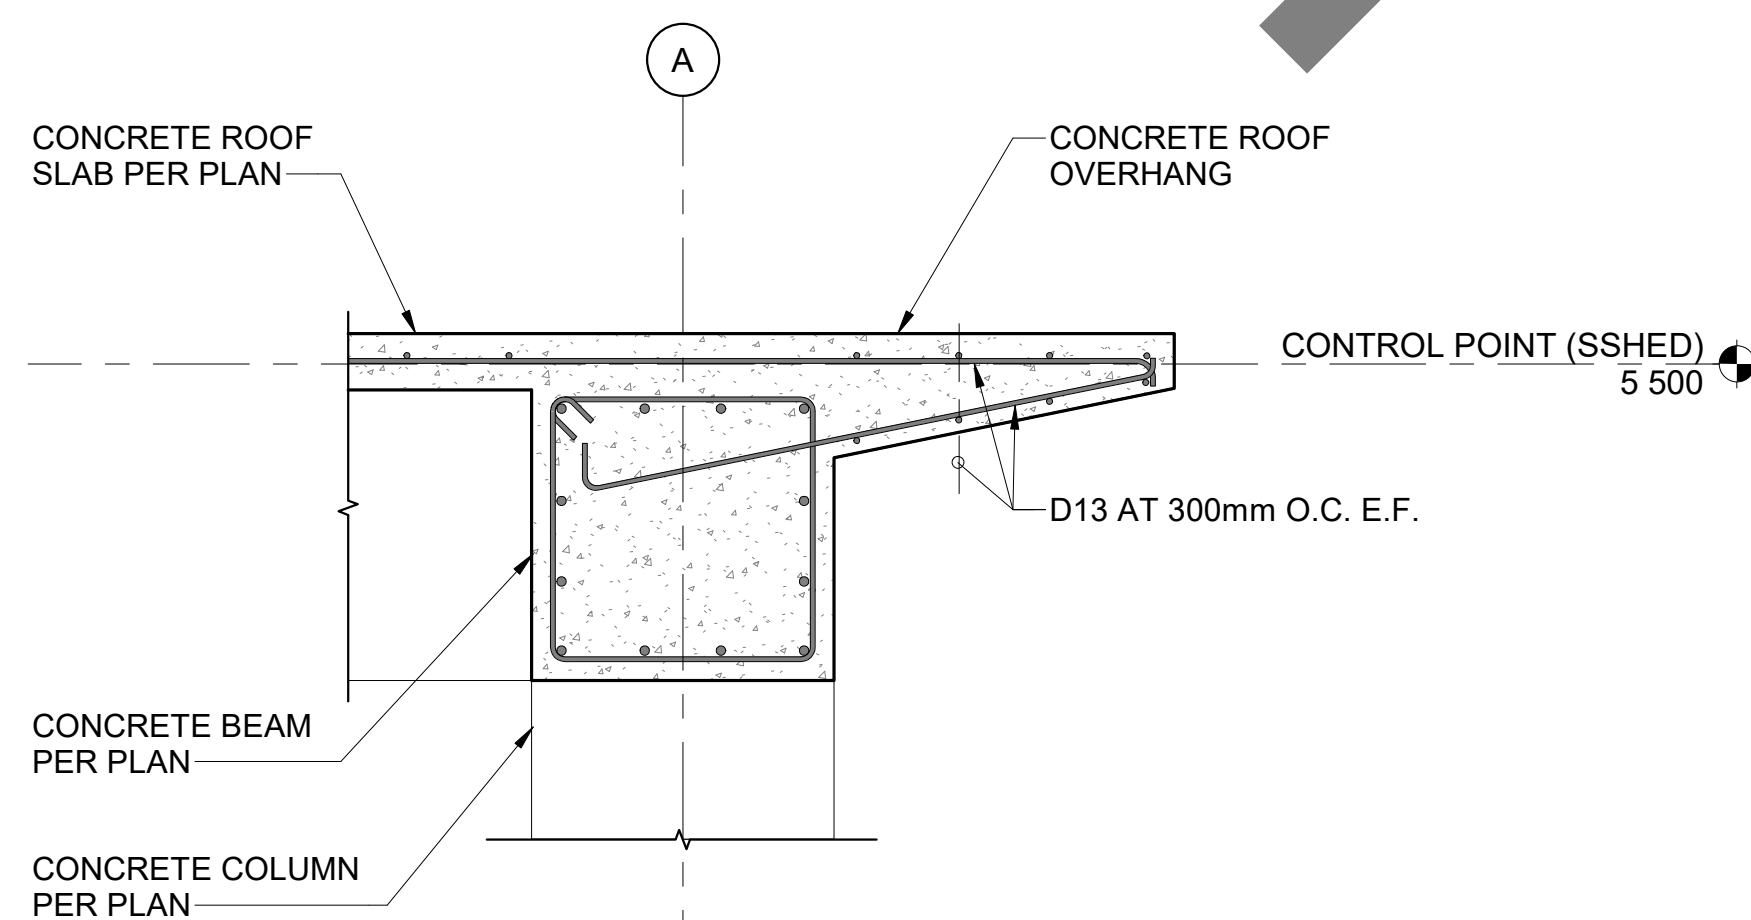



A9 OVERHANG DETAIL
SCALE 1 : 20

[illegible]


US ARMY CORPS OF ENGINEERS JAPAN ENGINEER DISTRICT OFFICE 10000 APO AP 96376-5133	DESIGNED BY: L. GARCHITO RENA	ISSUE DATE: JUNE 2018
	DRAWN BY: M. MIRA	SOLICITATION NO.:
 BSFM INTERNATIONAL, INC. 501 SUMNER STREET, SUITE 620 SAN FRANCISCO, CA 94111	ORDERED BY: J. UNO	CONTRACT NO.: W852N717-D-0083
	SUBMITTED BY: J. UNO	
	SIZE: 501 UNO	

APO AP 96343-5010
FY20 MCA PN77833 VEHICLE MAINTENANCE SHOP
BEAM PROFILE, SECTION AND DETAILS (CLIN
0004)


SHEET ID
SS
S-E503

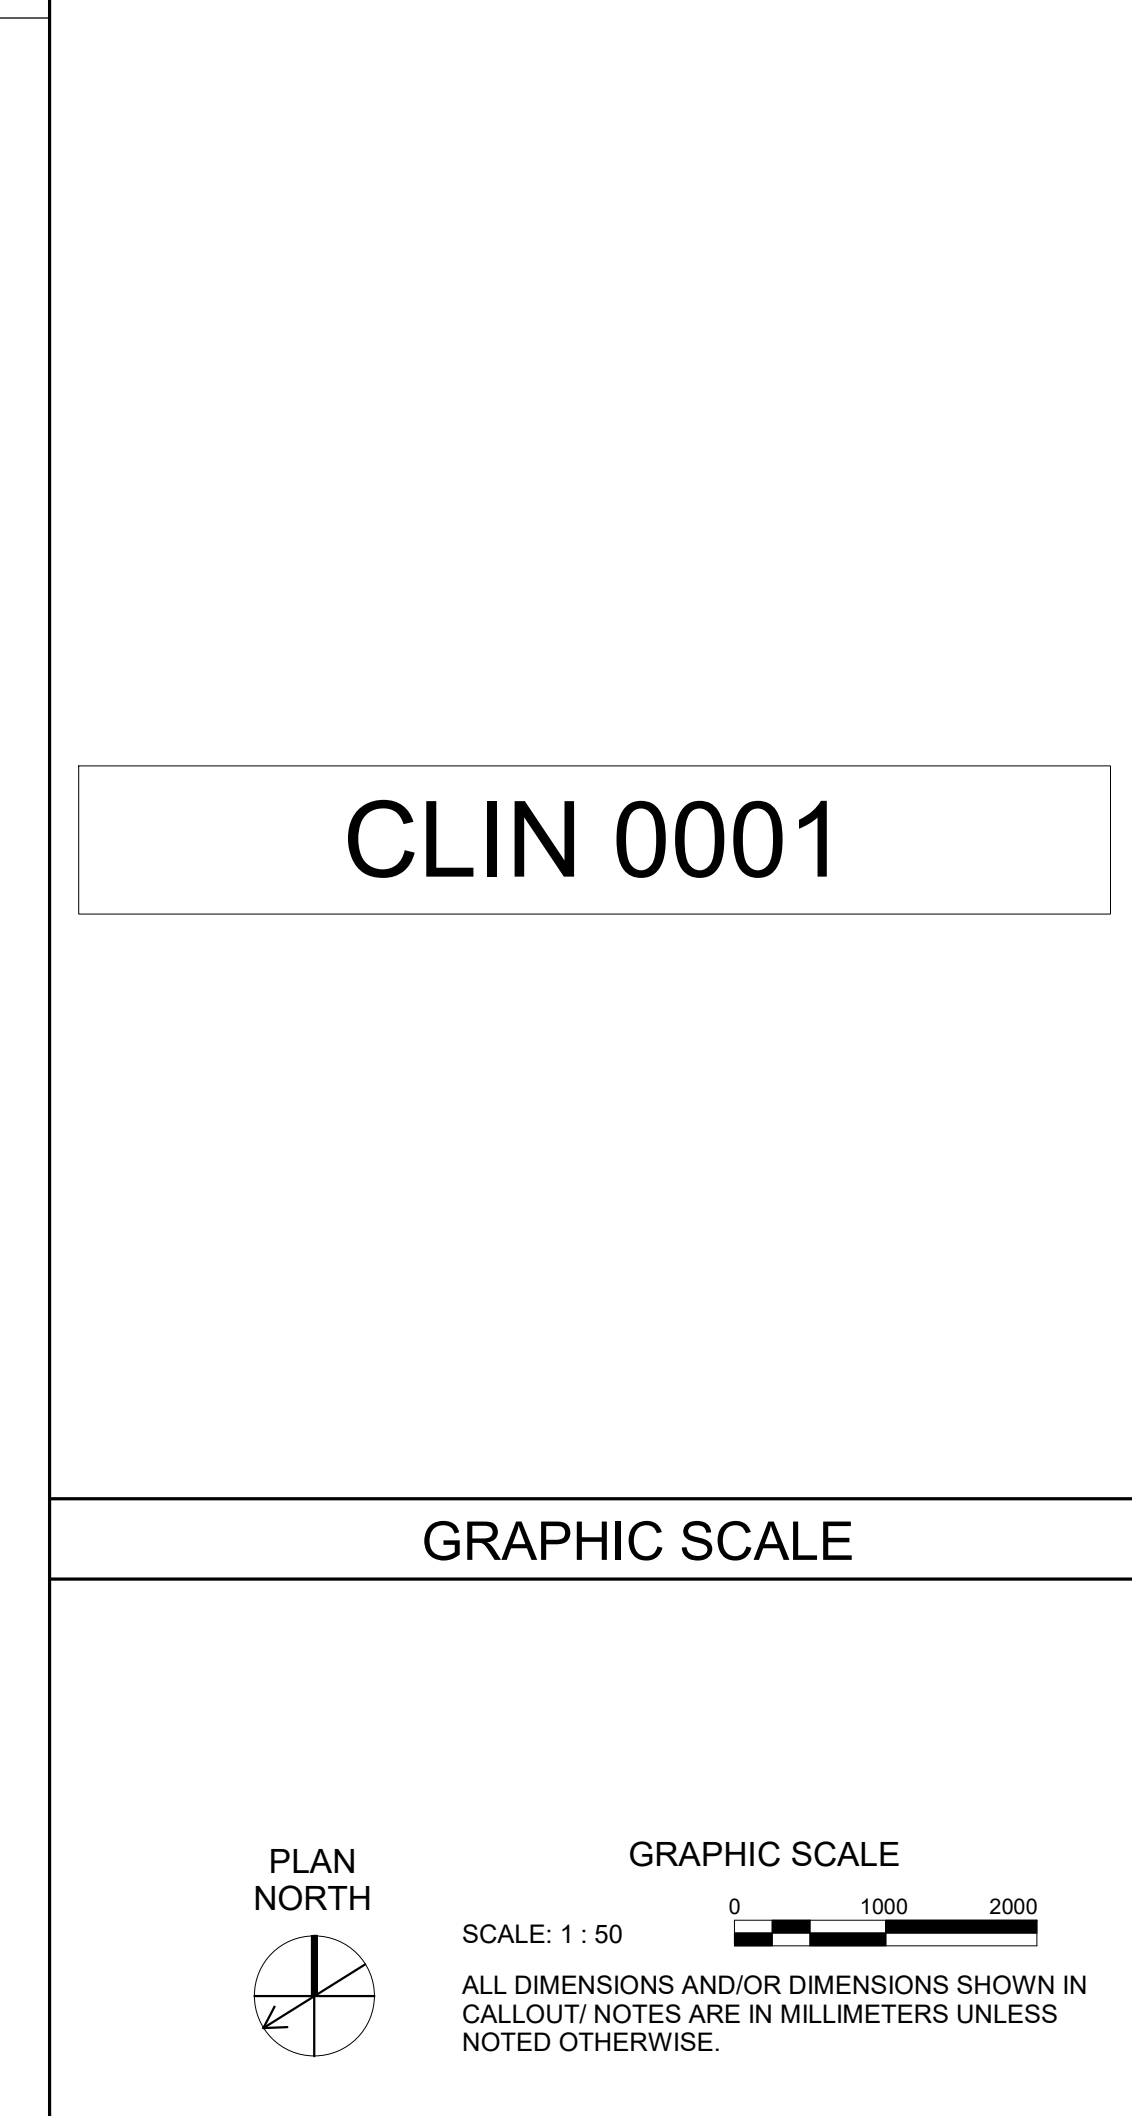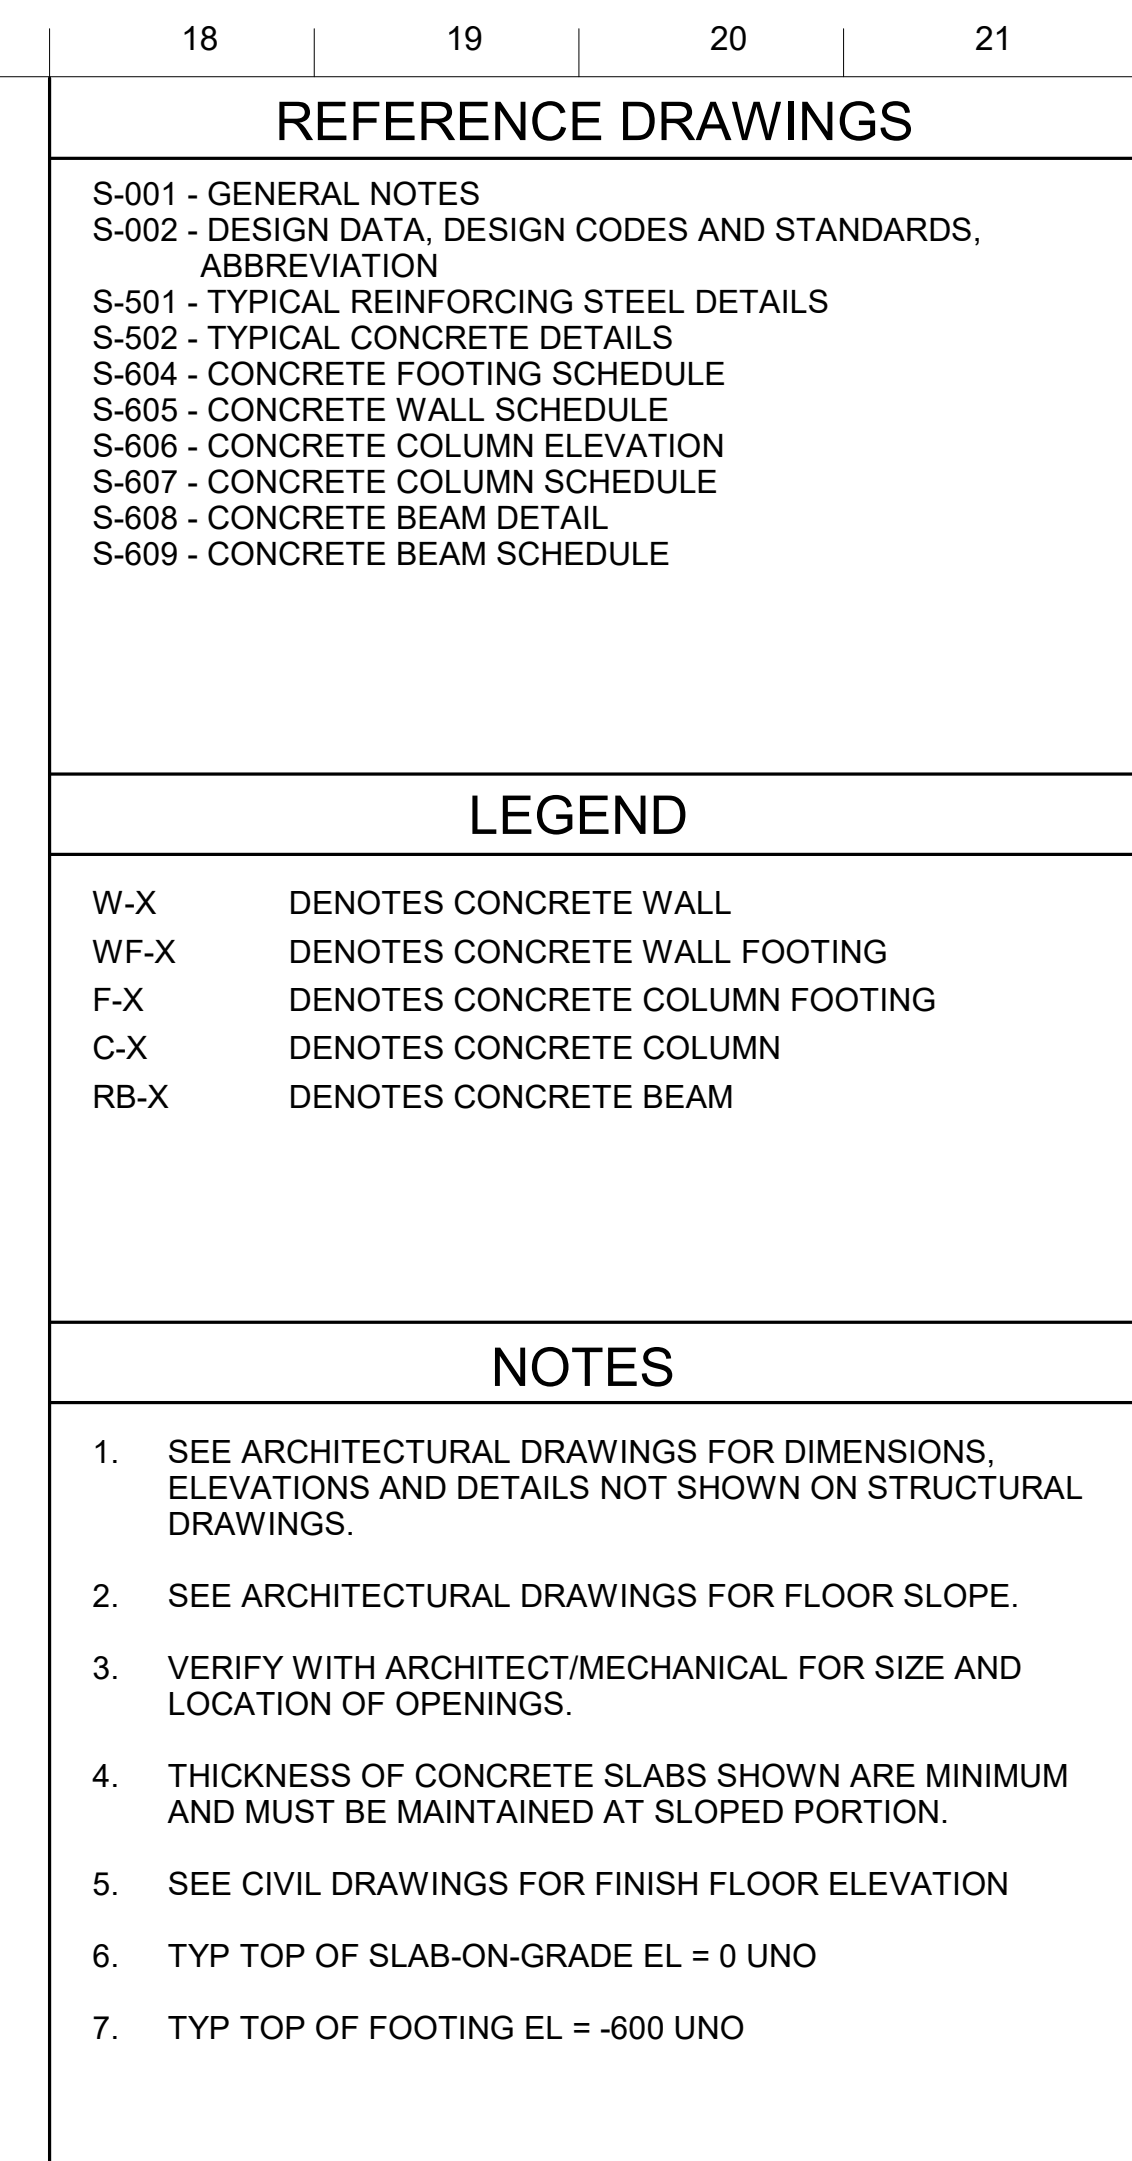


AFO AP 96343-5010 F20 MCA PN77833 (VEHICLE MAINTENANCE SHOP) FIRE PUMP BUILDING - FOUNDATION AND ROOF FRAMING PLAN (CLIN 0001)		SHEET ID FP S-F101	
US ARMY CORPS OF ENGINEERS JAPAN ENGINEER DISTRICT OKINAWA AREA OFFICE AFO AP 96376-5132		DESIGNED BY: K. PANG CHECKED BY: R. TANGNONAN J. UNO	
SSFM INTERNATIONAL, INC 501 SUMNER STREET, SUITE 620 HONOLULU, HAWAII 96817		ISSUE DATE: JUNE 2018 SOLICITATION NO.: CONTRACT NO.: W912HIV-17-D-0003 SUBMITTED BY: J. UNO	
		ANSI D	
		MARK	
		DESCRIPTION	
		DATE	

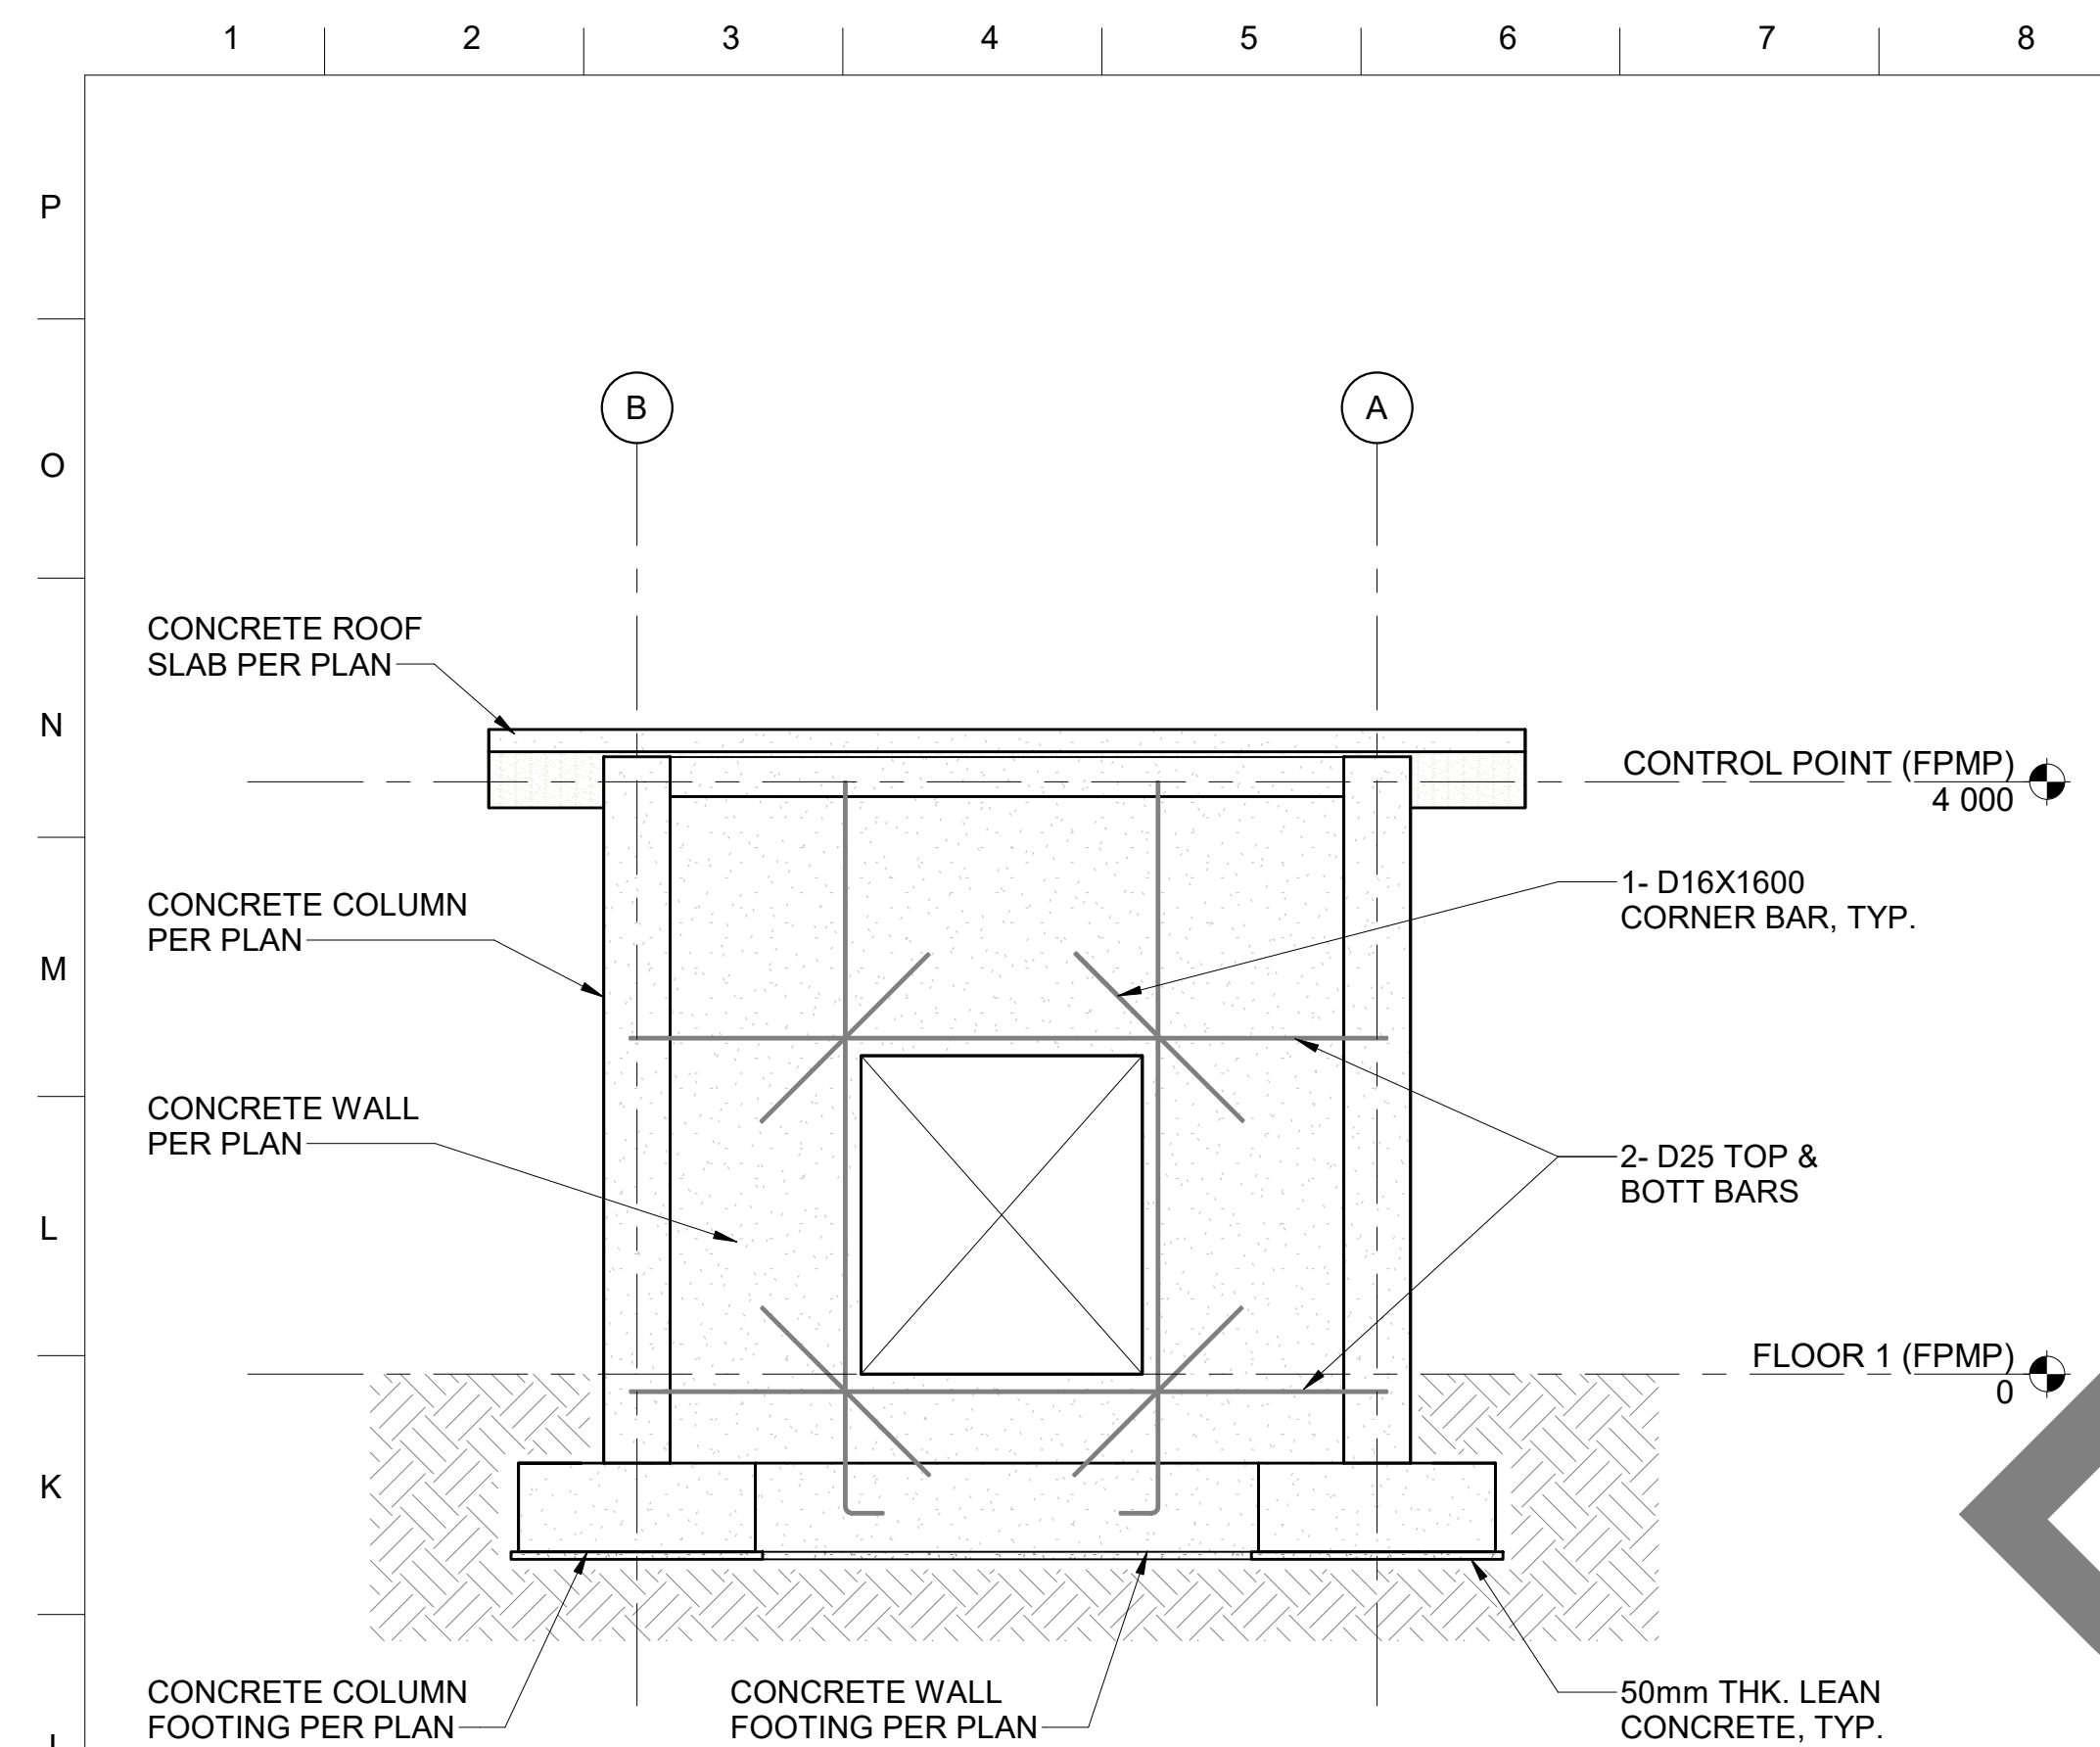


11 FP - EXTERIOR ELEVATION - EAST (CLIN 0001)
SCALE 1 : 50

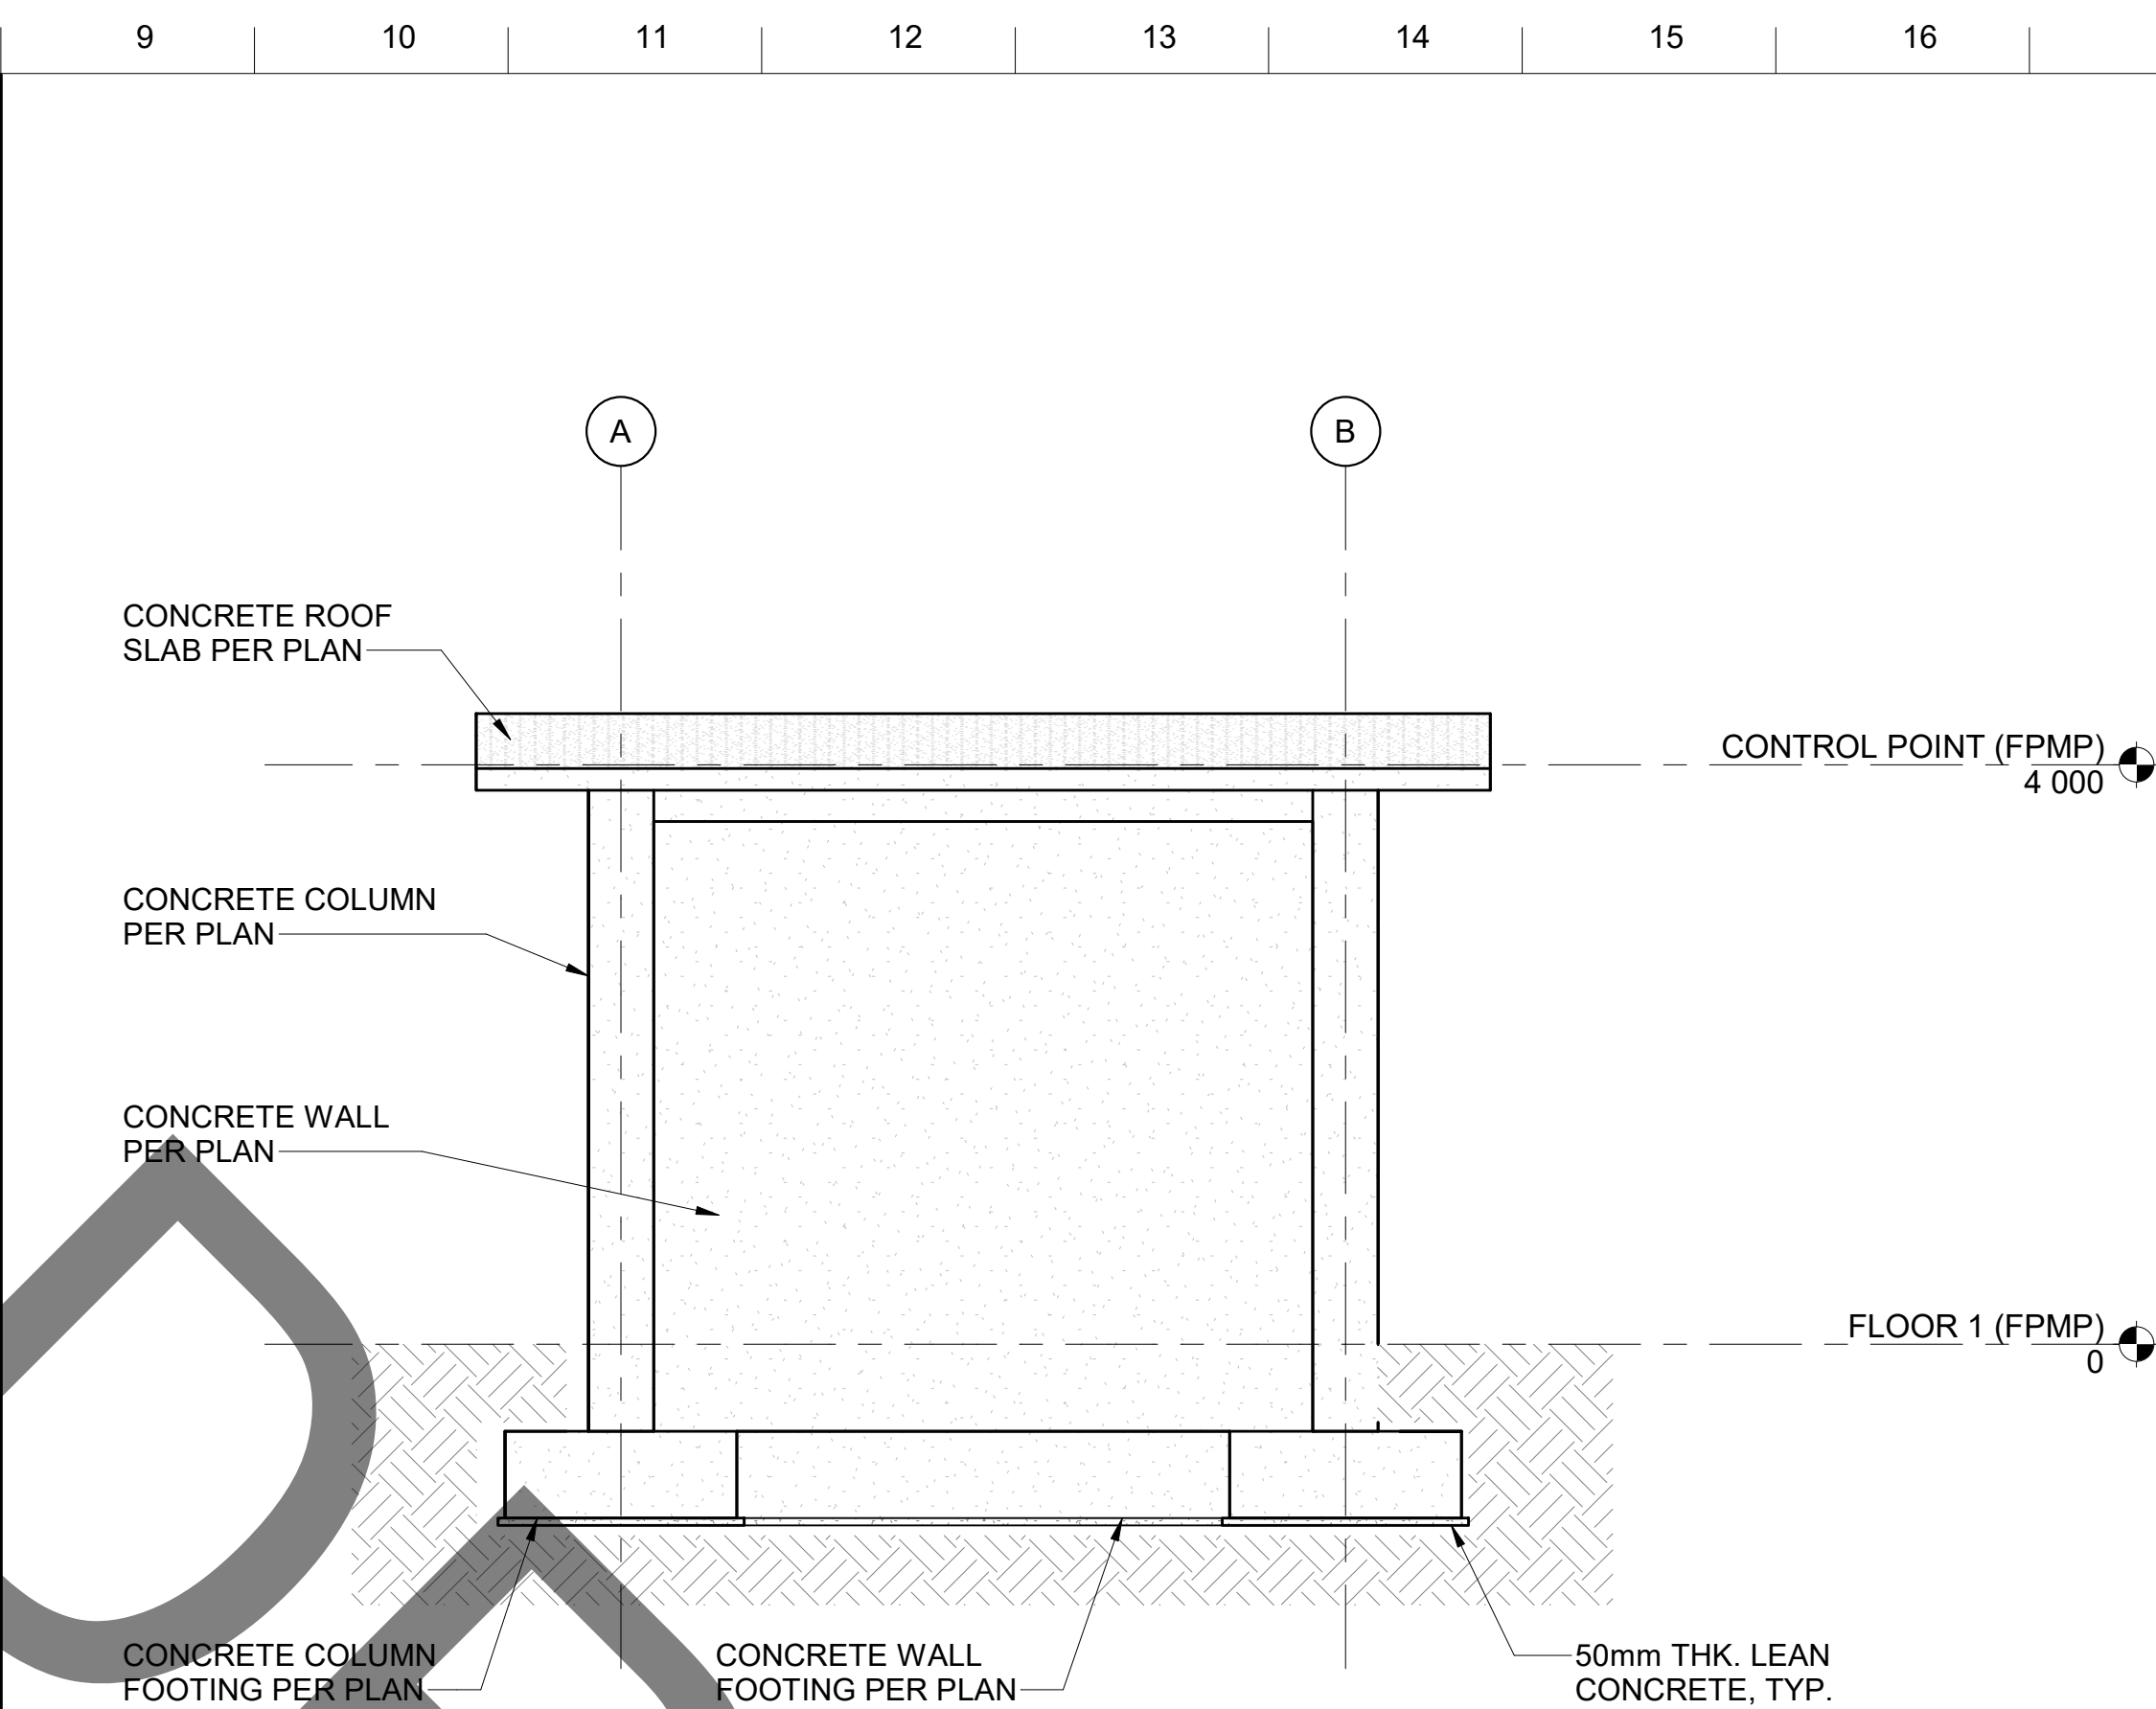

19 FP - EXTERIOR ELEVATION - WEST (CLIN 0001)
SCALE 1 : 50

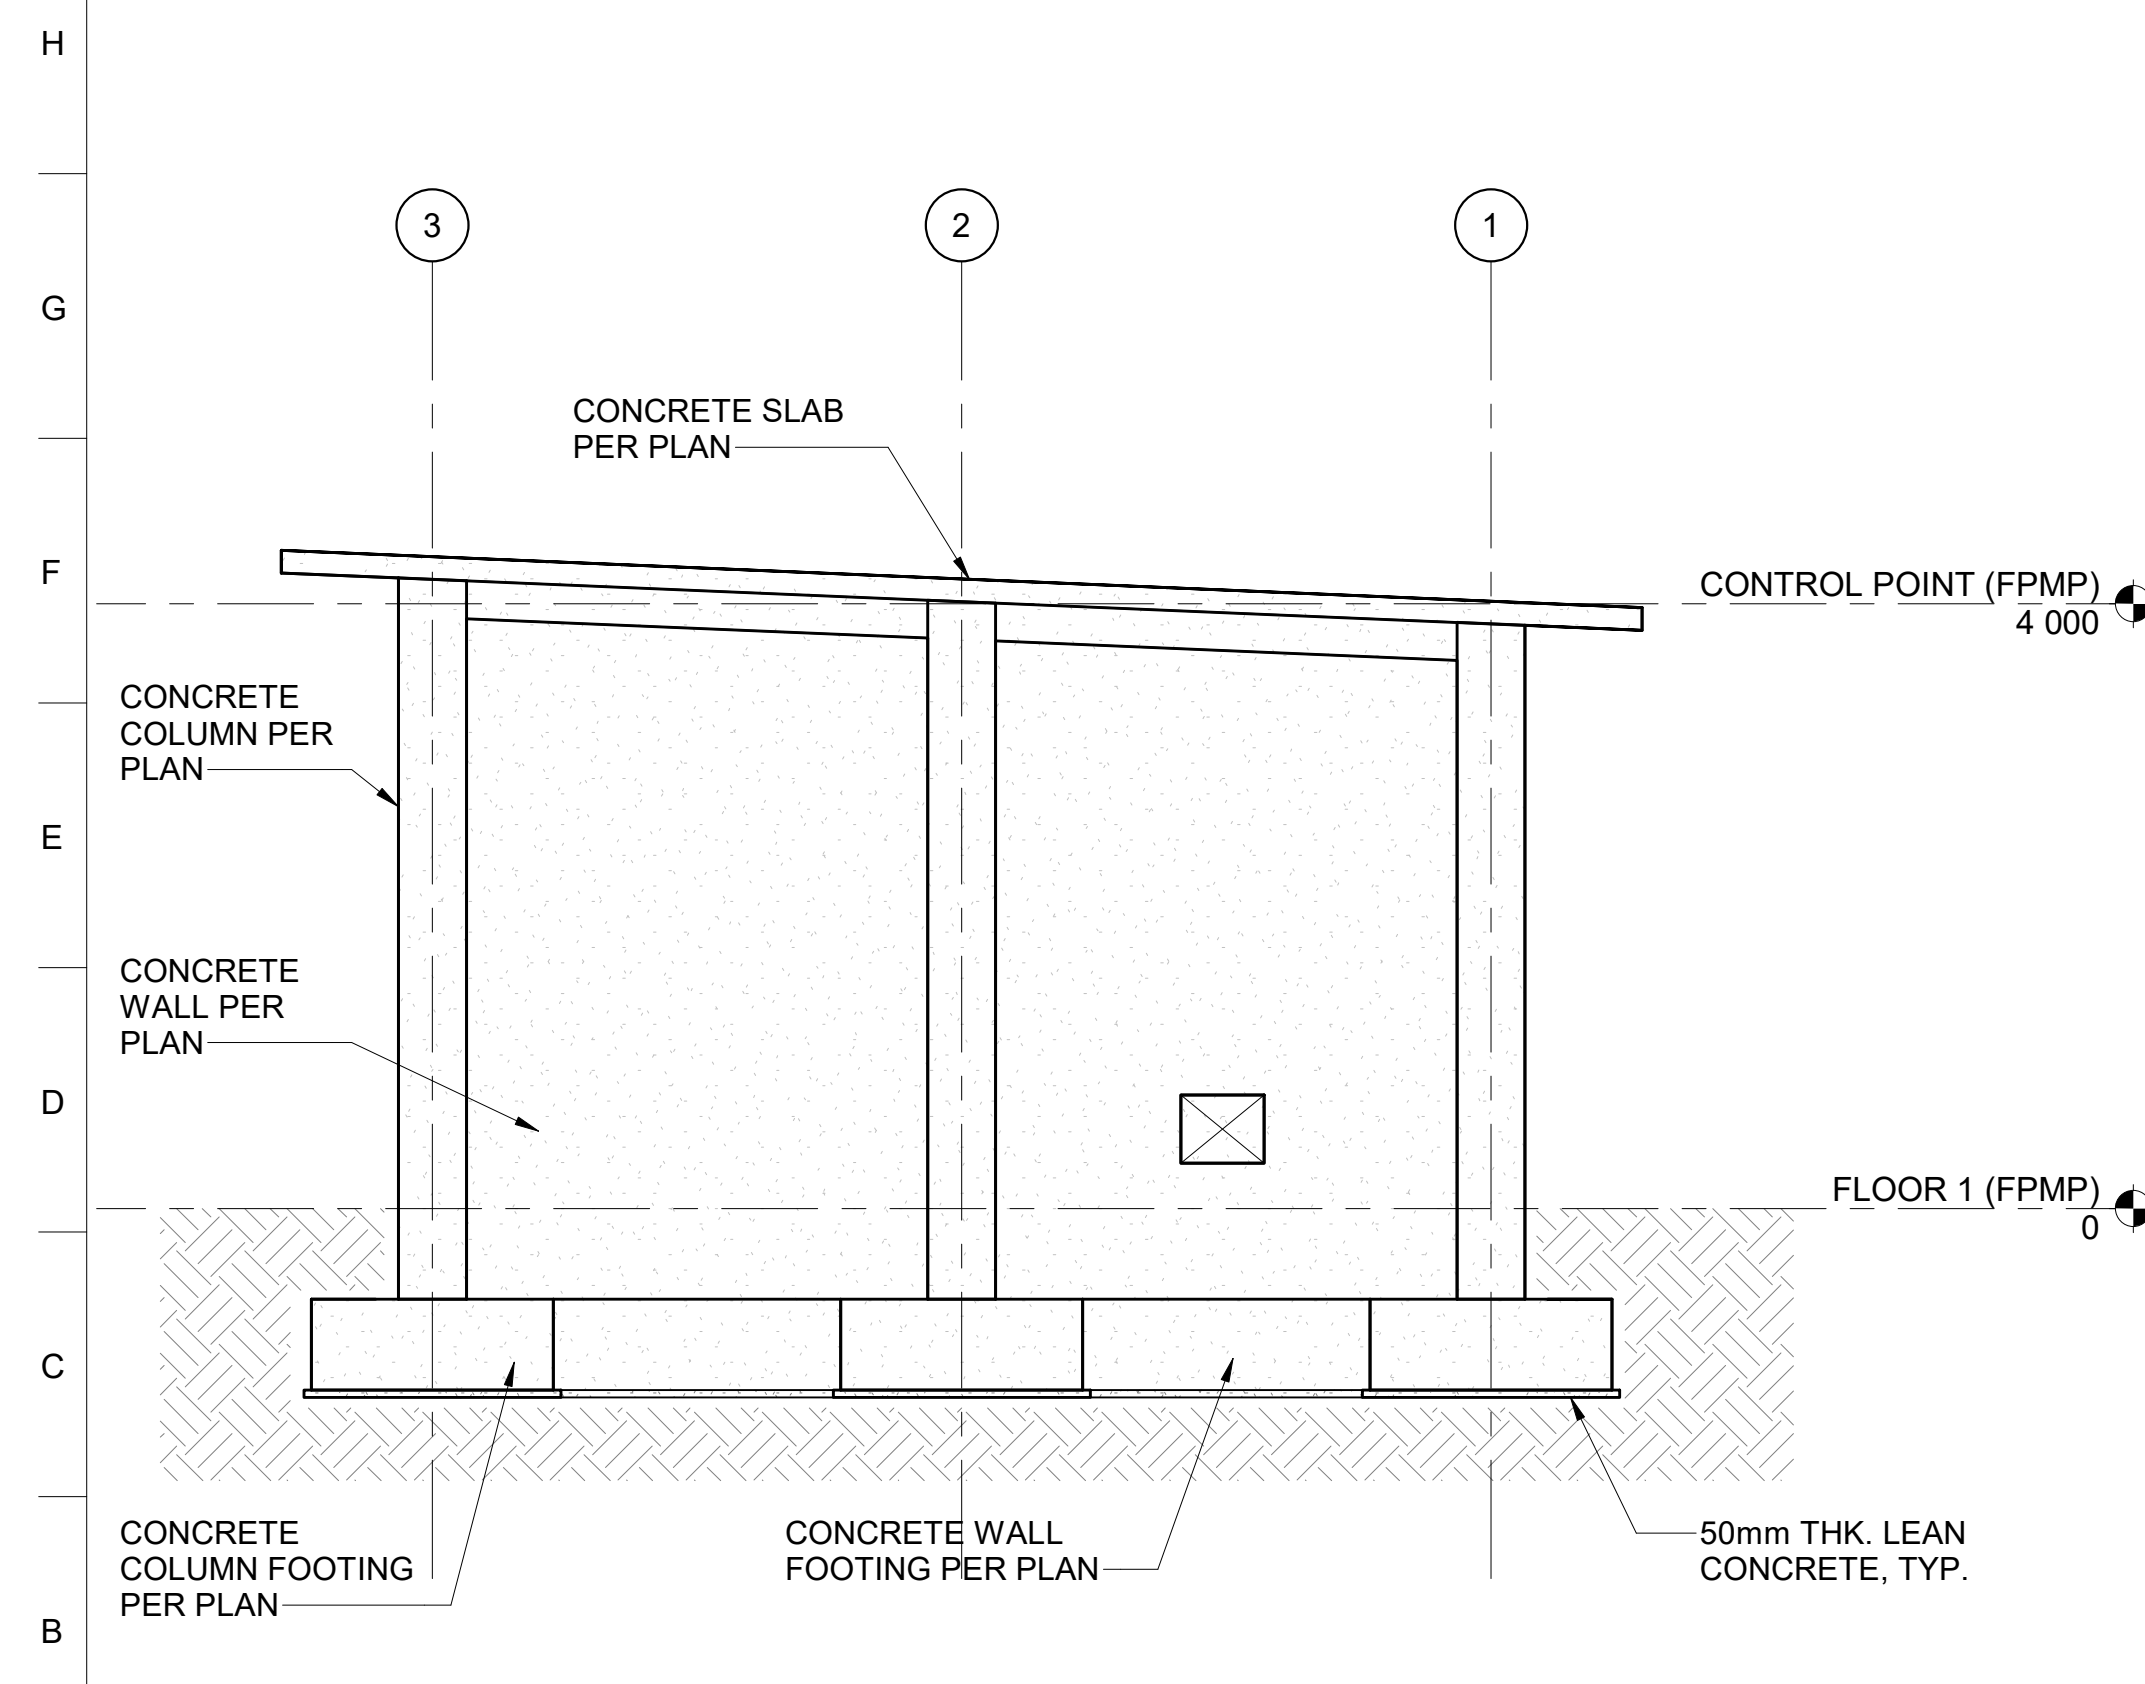

A1 FP - EXTERIOR ELEVATION - NORTH (CLIN 0001)
SCALE 1 : 50

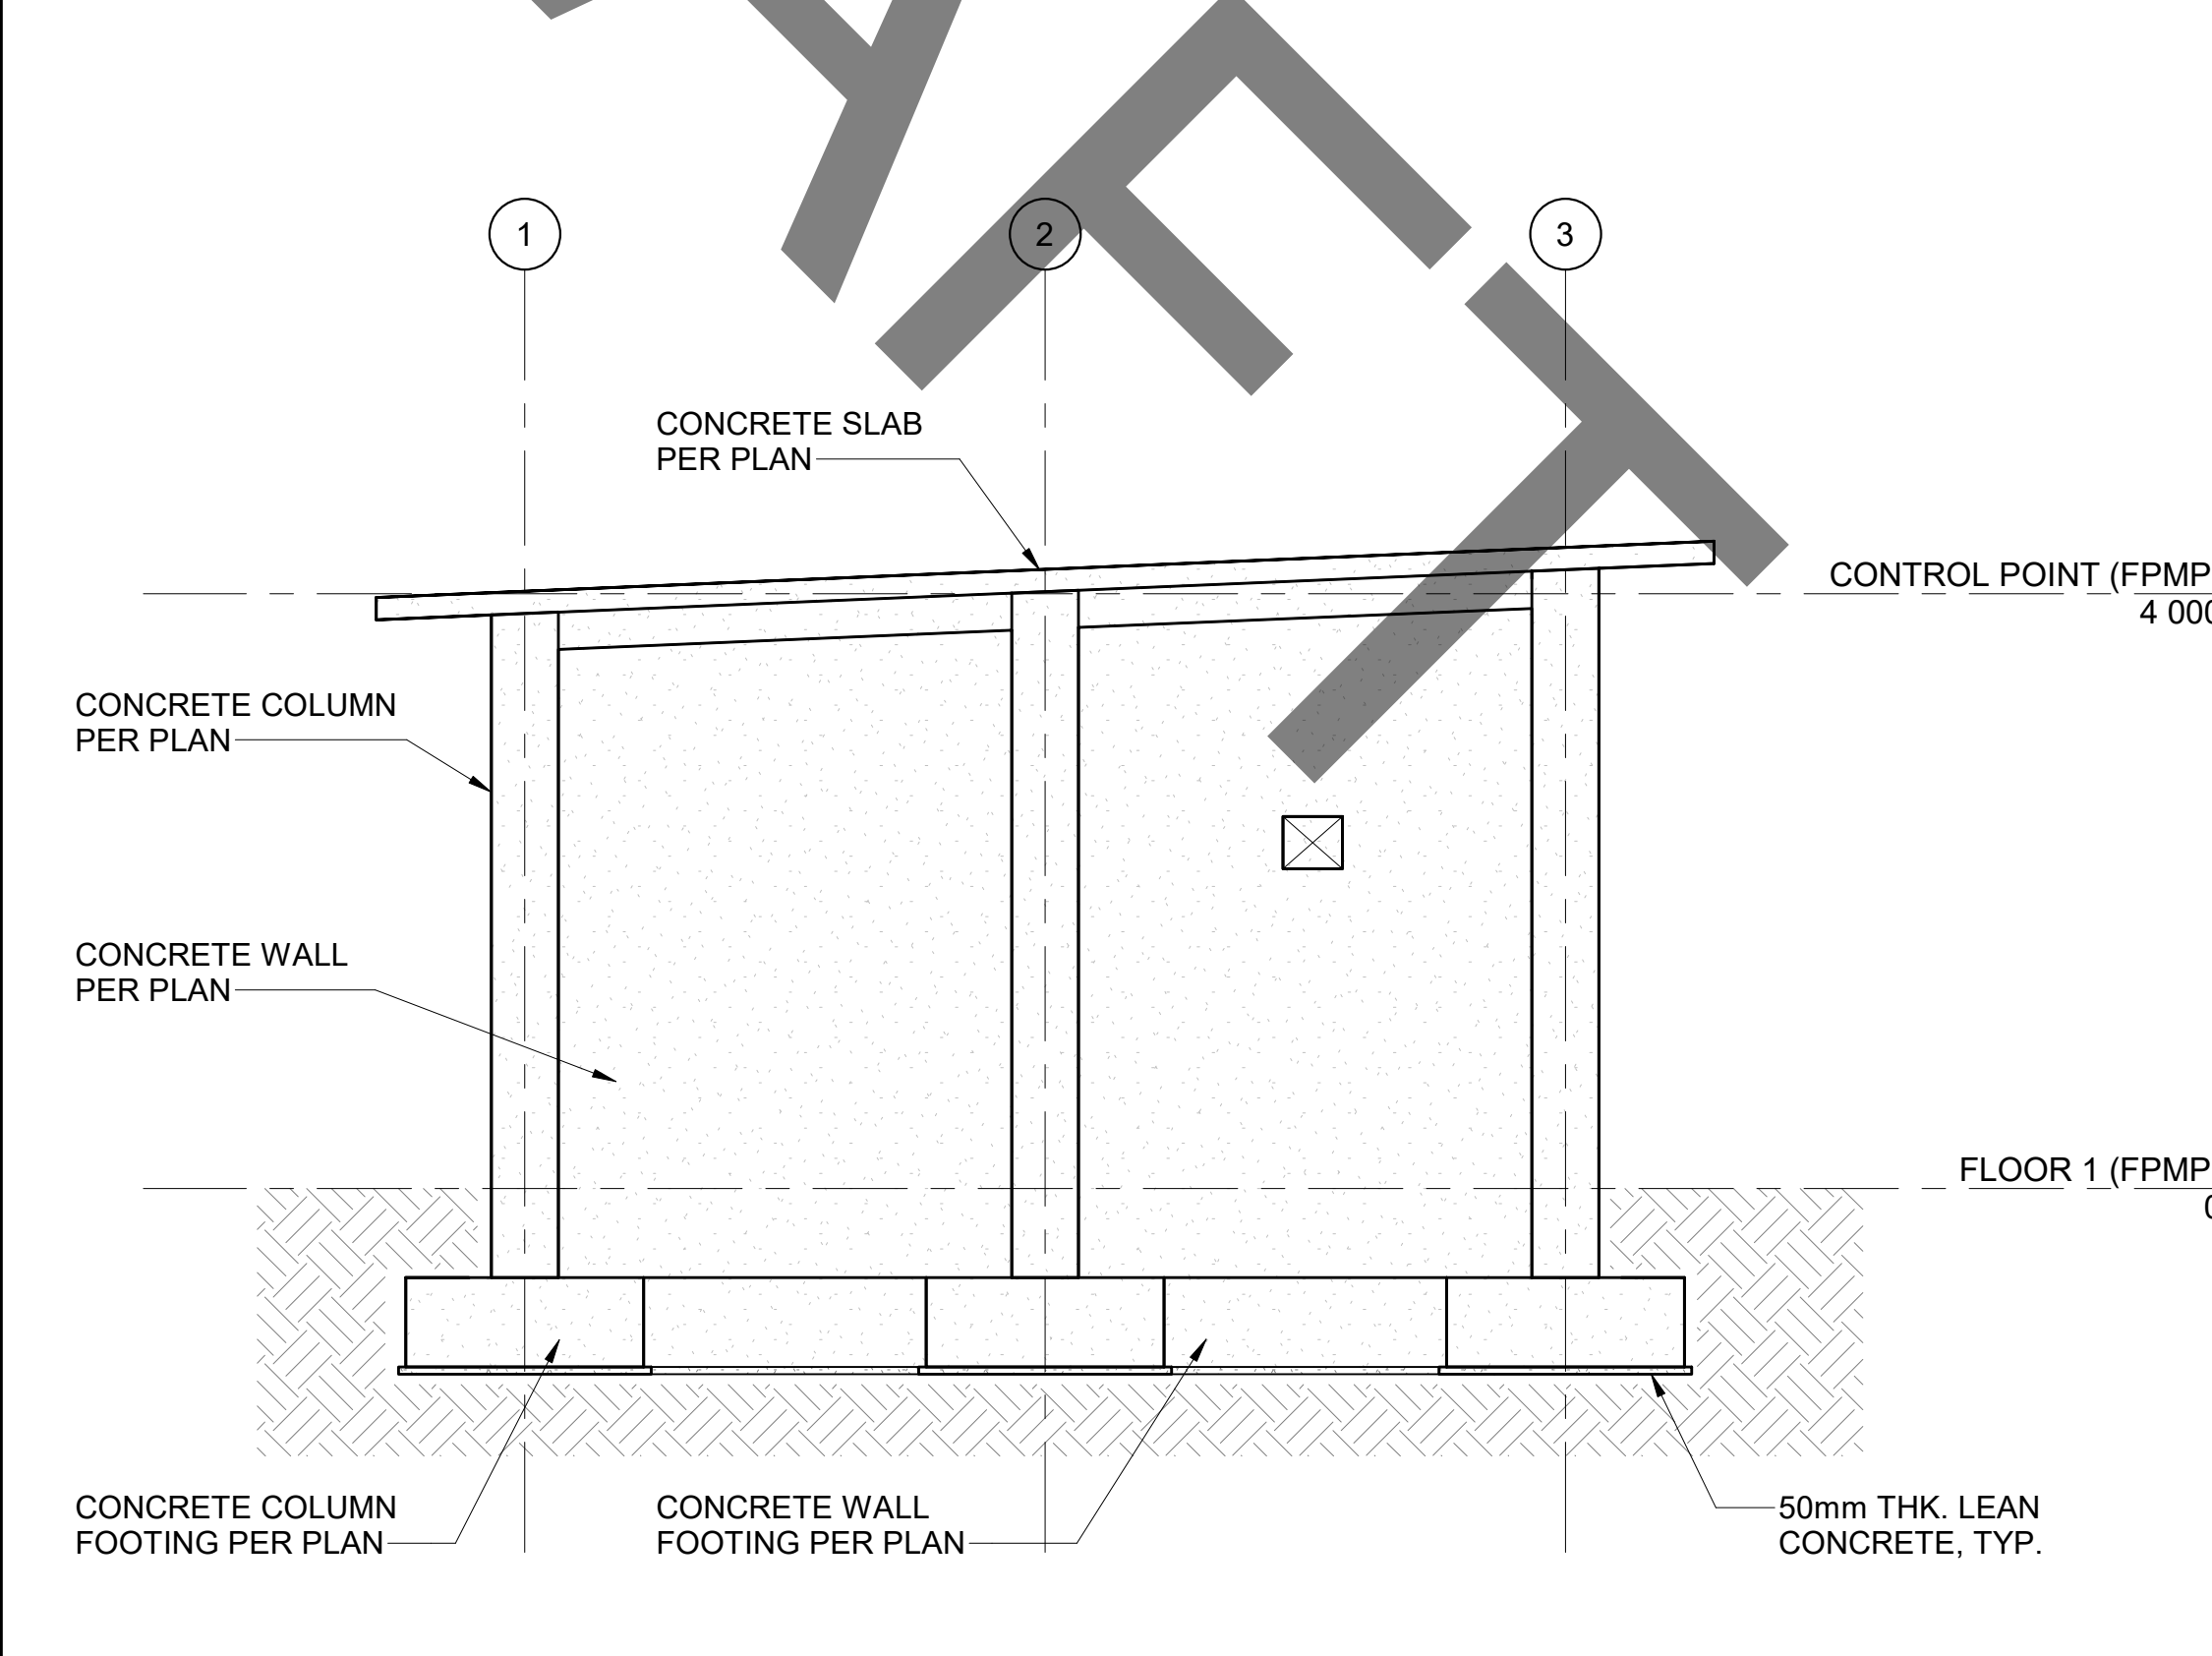

A9 FP - EXTERIOR ELEVATION - SOUTH (CLIN 0001)
SCALE 1 : 50

REFERENCE DRAWINGS

- S-001 - GENERAL NOTES
- S-002 - DESIGN DATA, DESIGN CODES AND STANDARDS ABBREVIATION
- S-501 - TYPICAL REINFORCING STEEL DETAILS
- S-502 - TYPICAL CONCRETE DETAILS
- S-604 - CONCRETE FOOTING SCHEDULE
- S-605 - CONCRETE WALL SCHEDULE
- S-606 - CONCRETE COLUMN ELEVATION
- S-607 - CONCRETE COLUMN SCHEDULE
- S-608 - CONCRETE BEAM DETAIL
- S-609 - CONCRETE BEAM SCHEDULE

LEGEND

W-X	DENOTES CONCRETE WALL
WF-X	DENOTES CONCRETE WALL FOOTING
F-X	DENOTES CONCRETE COLUMN FOOTING
C-X	DENOTES CONCRETE COLUMN
RB-X	DENOTES CONCRETE BEAM

NOTES

1. SEE ARCHITECTURAL DRAWINGS FOR DIMENSIONS, ELEVATIONS AND DETAILS NOT SHOWN ON STRUCTURAL DRAWINGS.
2. SEE ARCHITECTURAL DRAWINGS FOR FLOOR SLOPE.
3. VERIFY WITH ARCHITECT/MECHANICAL FOR SIZE AND LOCATION OF OPENINGS.



US Army Corps
of Engineers ®

[illegible]

ISSUED BY: K. PANG DATE: JUNE 2018	SOLICITATION NO.:
DRAWN BY: R. TANGMANON DATE: MAY 2018	CONTRACT NO.: W9127N-17-2-0083
CHECKED BY: 	SUBMITTED BY: J. UNO
SIZE: ANSI D	

Autodesk Docs: \\Vehicle Maint Shop Kadena\511758_TEMF_STRUC.rvt

File Path:

Plot Date: 12/16/2025 3:37:37 PM

INTERMEDIATE DESIGN

833 VEHICLE MAINTENANCE SHOP

FY20 MCA PN77833 VEHICLE MAINTENANCE SHOP

FIRE PUMP BUILDING - EXTERIOR ELEVATIONS
(CLIN 0001)

SHEET ID

FP
-F201

CLIN 0001



GRAPHIC SCALE


0 1000 2000

SCALE: 1 : 50



ALL DIMENSIONS AND/OR DIMENSIONS SHOWN IN
CALLOUT/ NOTES ARE IN MILLIMETERS UNLESS
NOTED OTHERWISE.

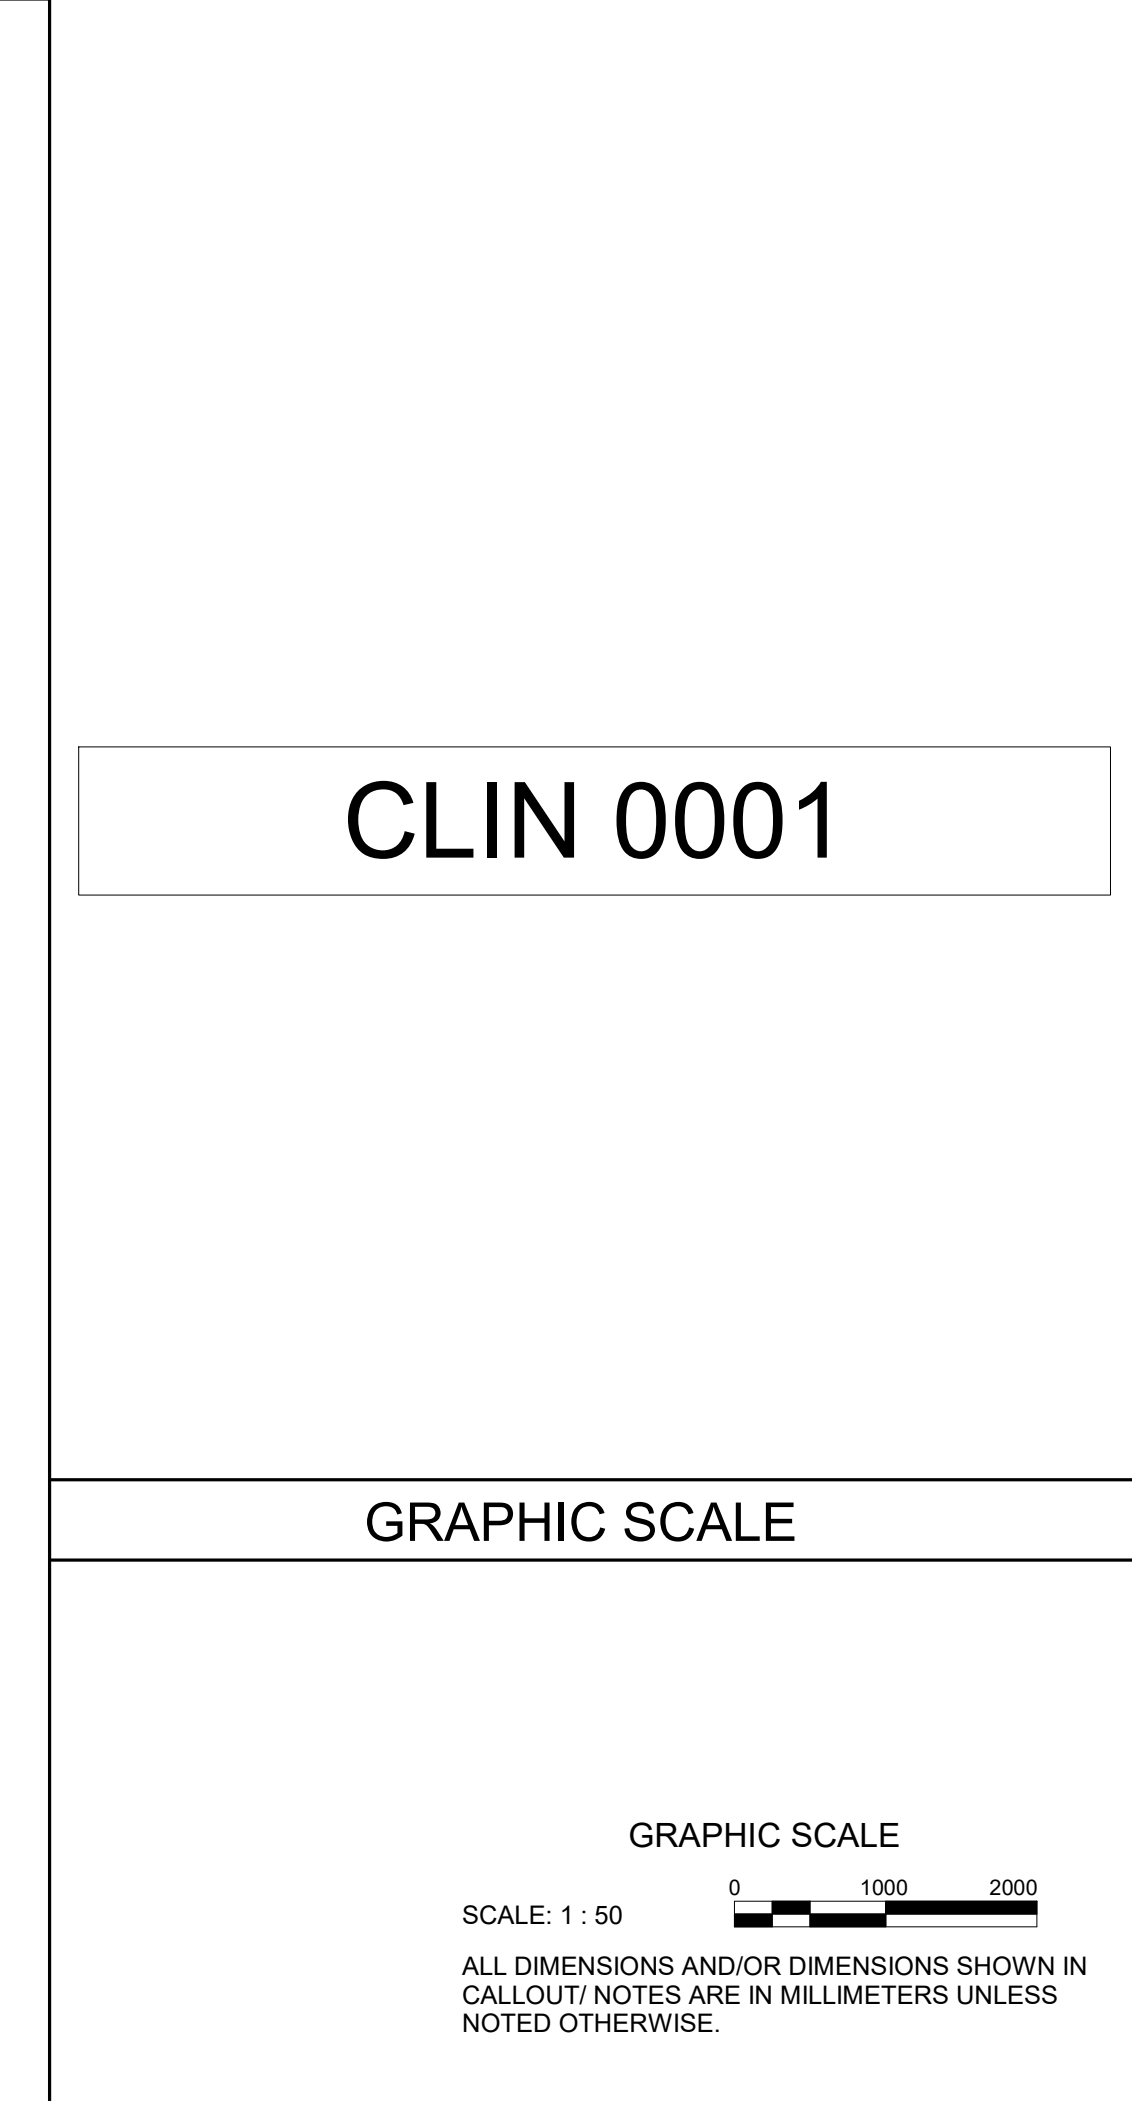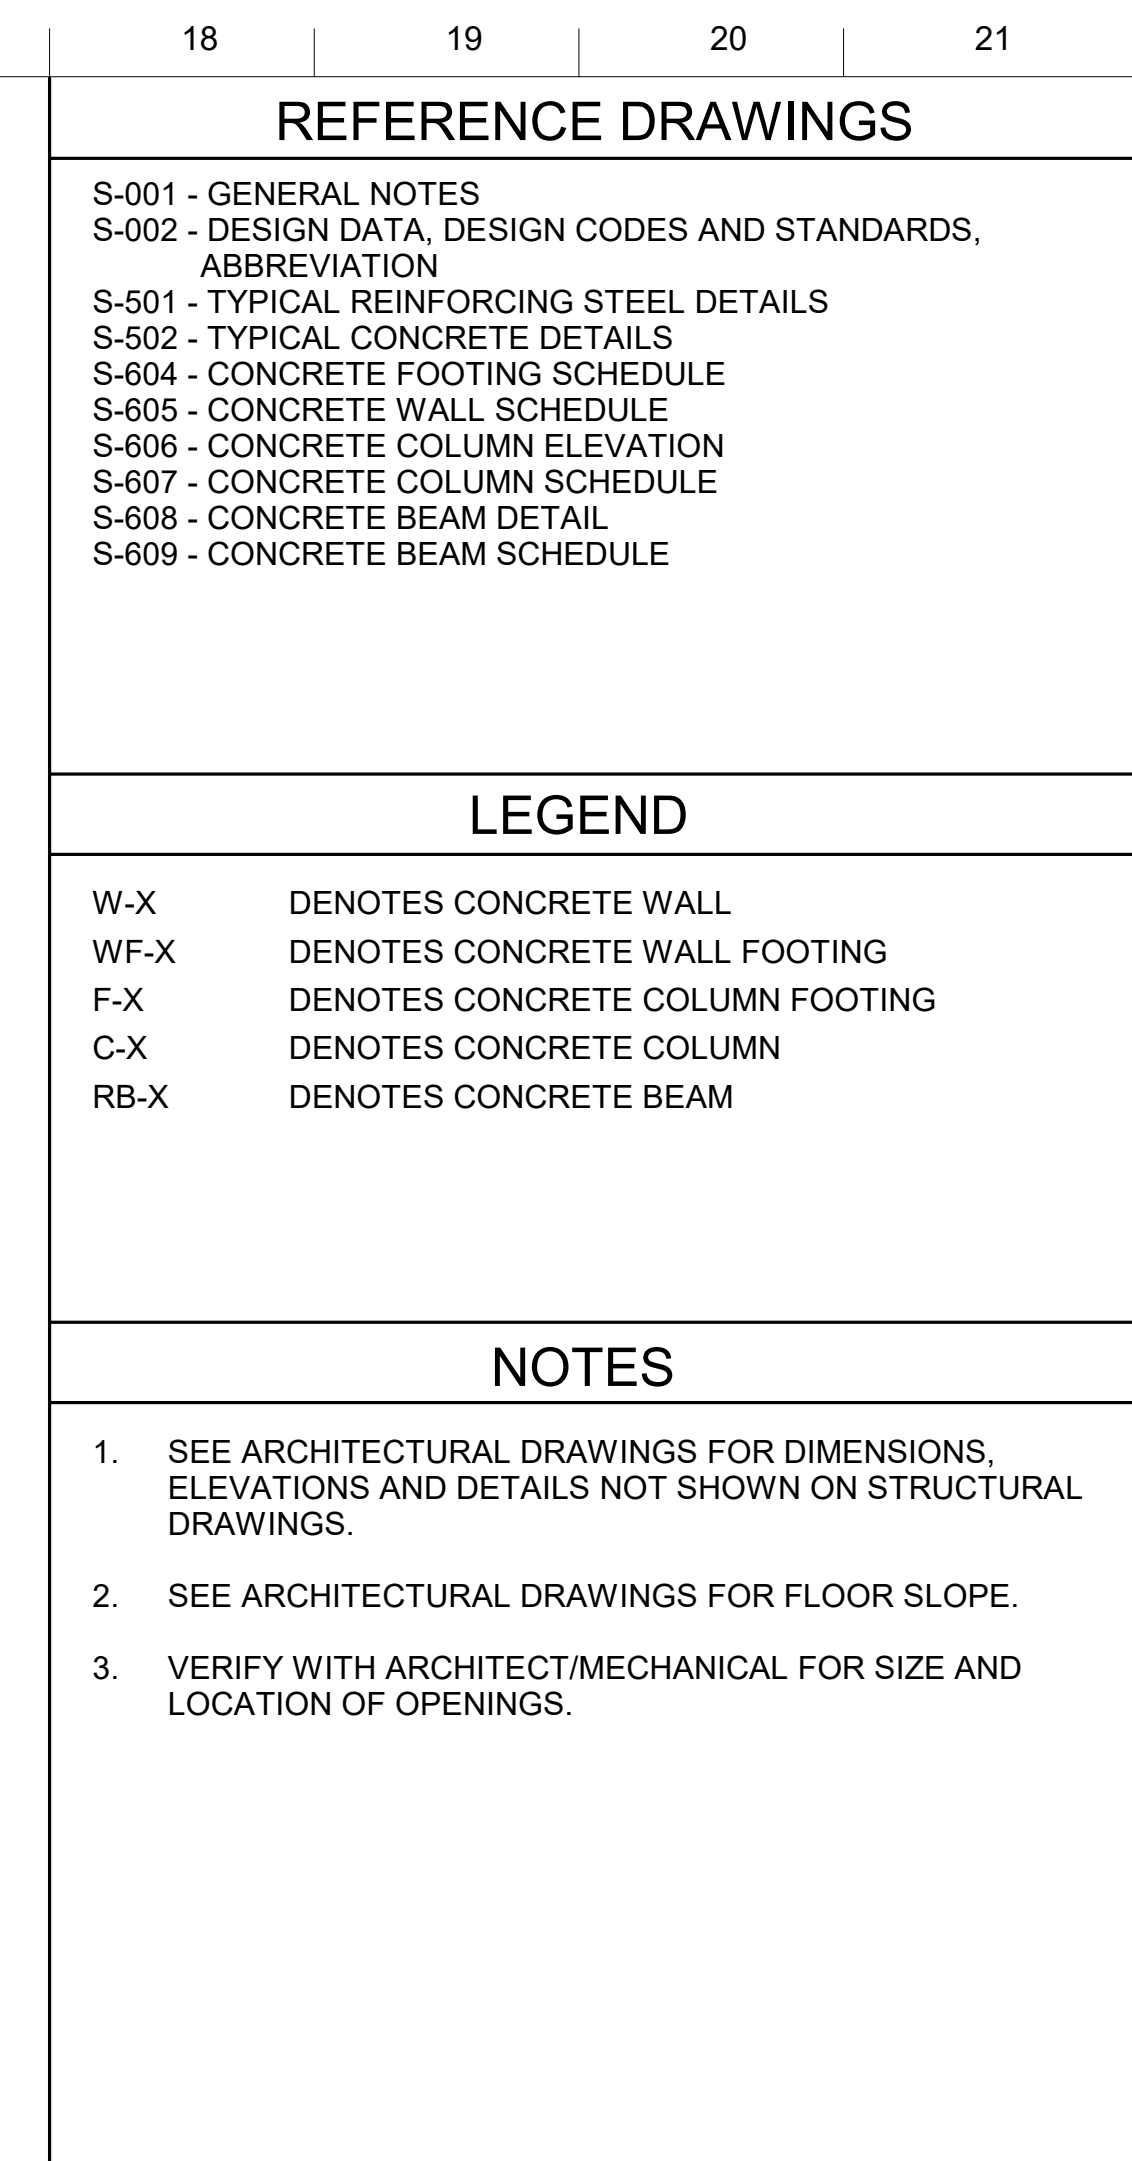[illegible]

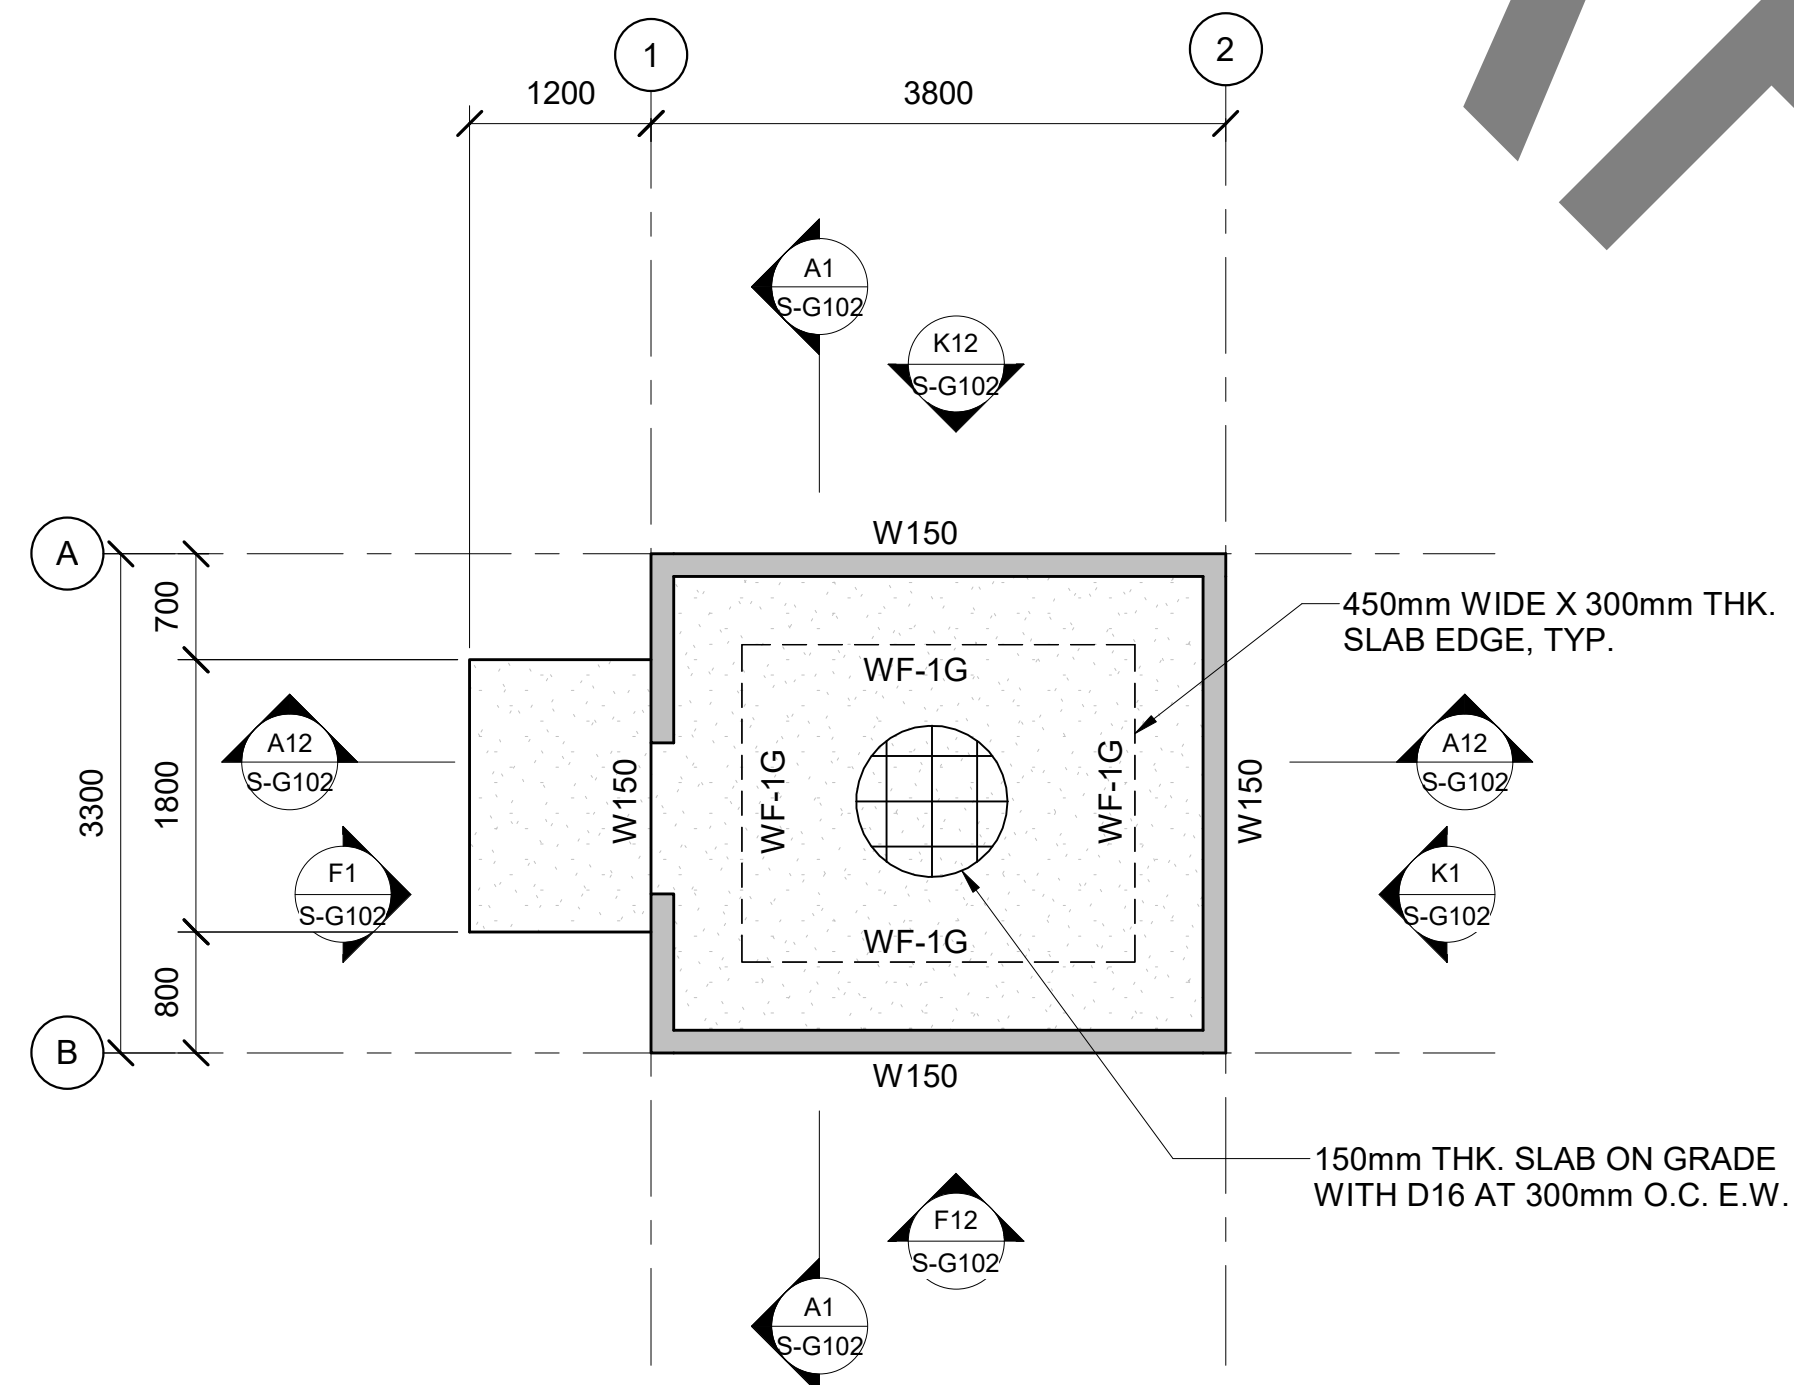


A1 CH - FOUNDATION PLAN (CLIN 0001)
SCALE 1 : 50

NOTES

1. SEE ARCHITECTURAL DRAWINGS FOR DIMENSIONS, ELEVATIONS AND DETAILS NOT SHOWN ON STRUCTURAL DRAWINGS.
2. SEE ARCHITECTURAL DRAWINGS FOR FLOOR SLOPE.
3. VERIFY WITH ARCHITECT/MECHANICAL FOR SIZE AND LOCATION OF OPENINGS.
4. THICKNESS OF CONCRETE SLABS SHOWN ARE MINIMUM AND MUST BE MAINTAINED AT SLOPED PORTION.
5. SEE CIVIL DRAWINGS FOR FINISH FLOOR ELEVATION.
6. TYP TOP OF SLAB-ONGRADE EL = 0 UNO
7. TYP TOP OF FOOTING EL = -600 UNO

GRAPHIC SCALE

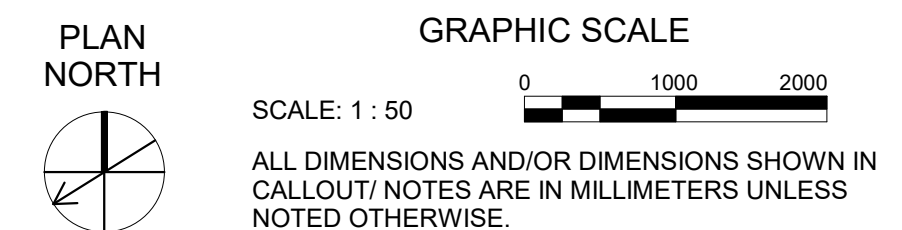


U.S. ARMY CORPS OF ENGINEERS DISTRICT ENGINEER KOKINAWA AREA OFFICE APO AP 96376-5132	DESIGNED BY: J. L. BRYAN DRAWN BY: R. TANGOMAN CHECKED BY: J. UNO	ISSUE DATE: JUNE 2016 SOLICITATION NO.: CONTRACT NO.: W912H1-17-D-0003
 SSFM INTERNATIONAL, INC. 505 KALANANUI AVE., SUITE 420 HONOLULU, HAWAII 96817	SUBMITTED BY: SSFM INTERNATIONAL, INC. 505 KALANANUI AVE., SUITE 420 HONOLULU, HAWAII 96817	DATE: SIZE: ANSI D


F-Y20 MCA PN77833 VEHICLE MAINTENANCE SHOP

CABLE HUT FOUNDATION AND ROOF FRAMING
PLAN (CLIN 0001)


SHEET ID
CH
-G101

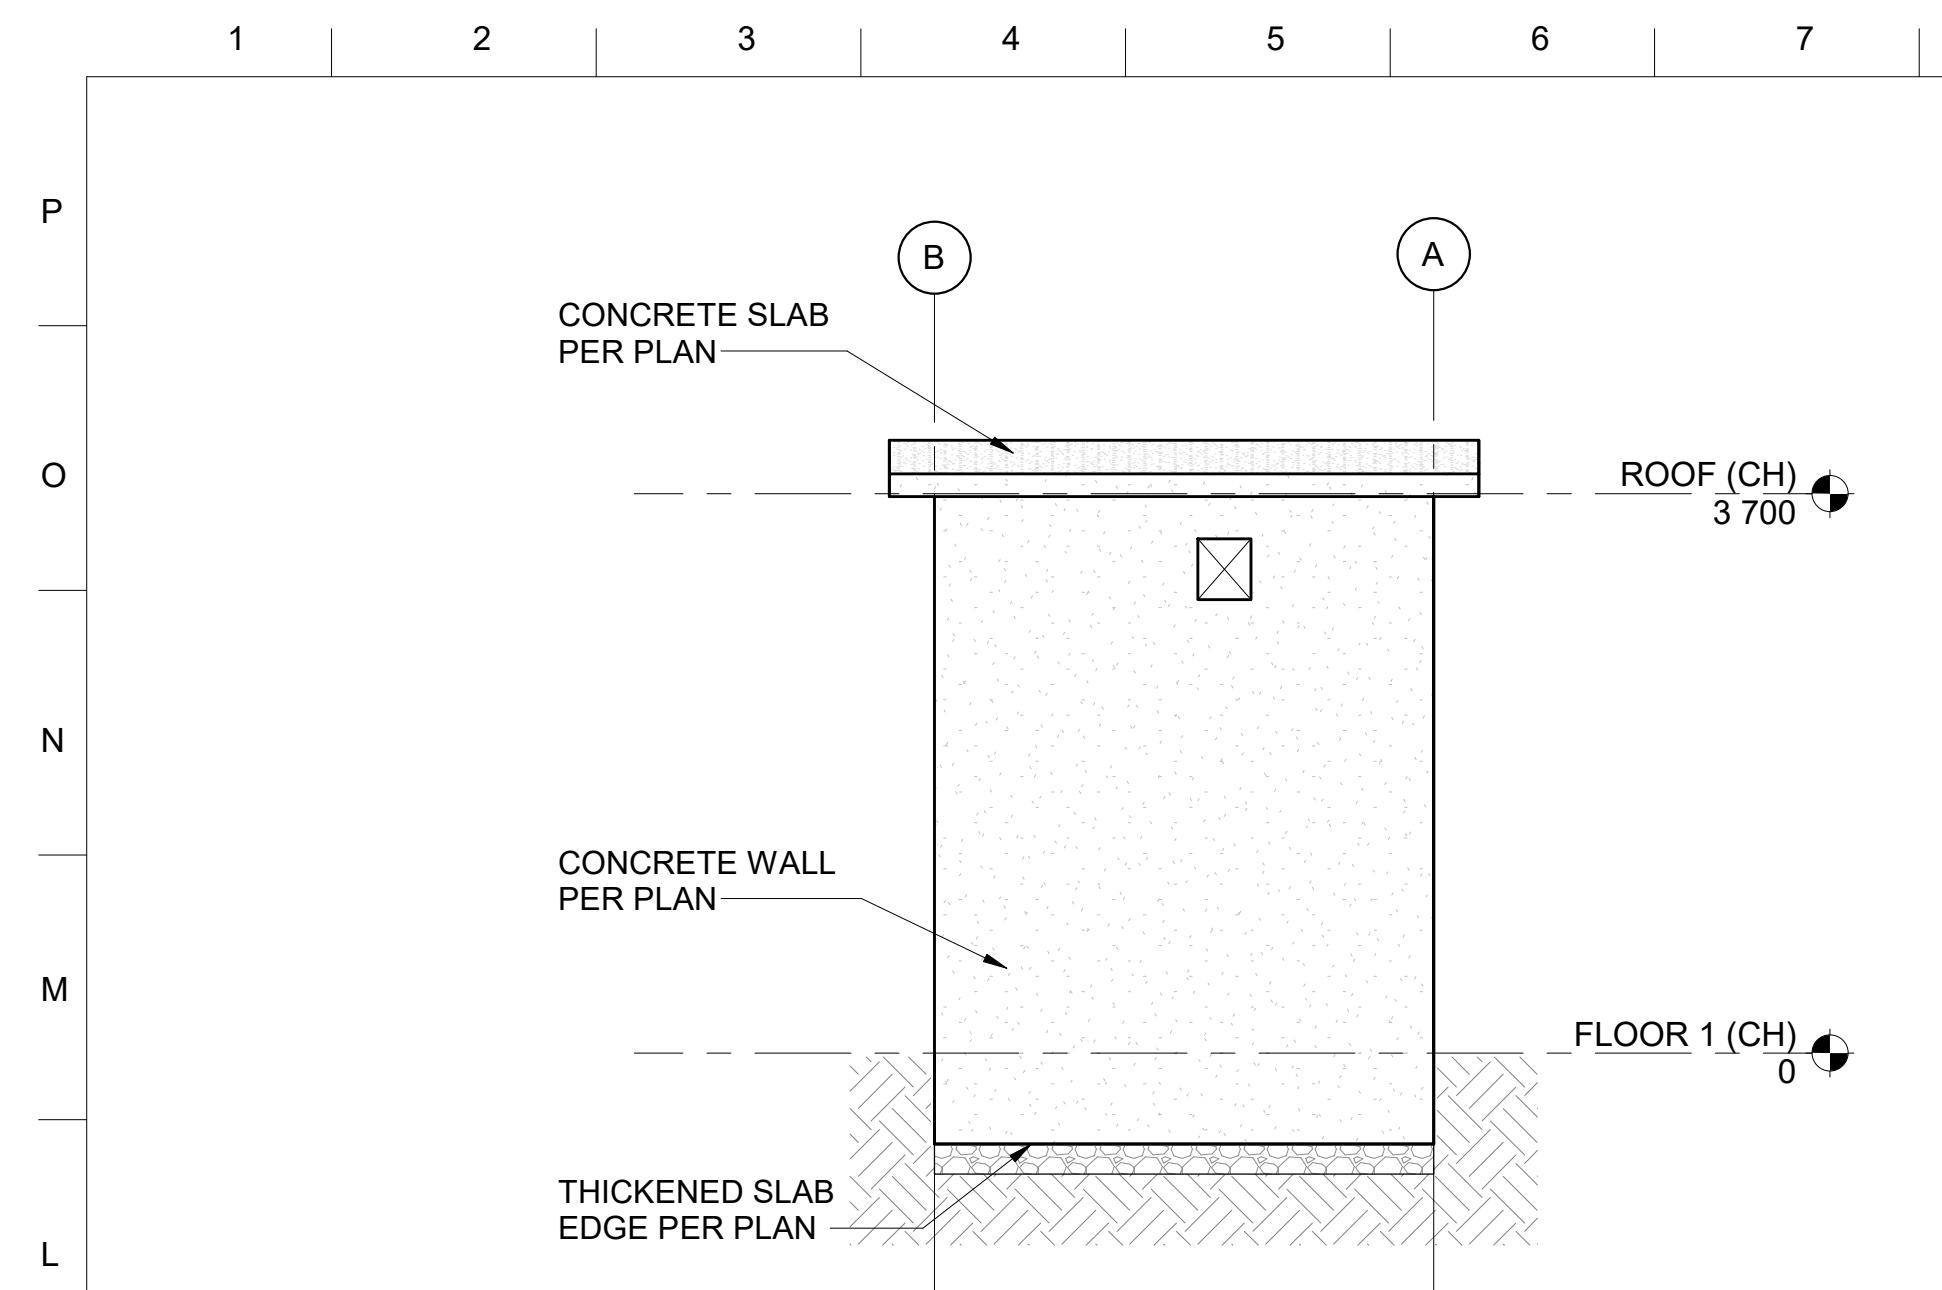


K1 CH - EXTERIOR ELEVATION - EAST (CLIN 0001)
SCALE 1 : 50

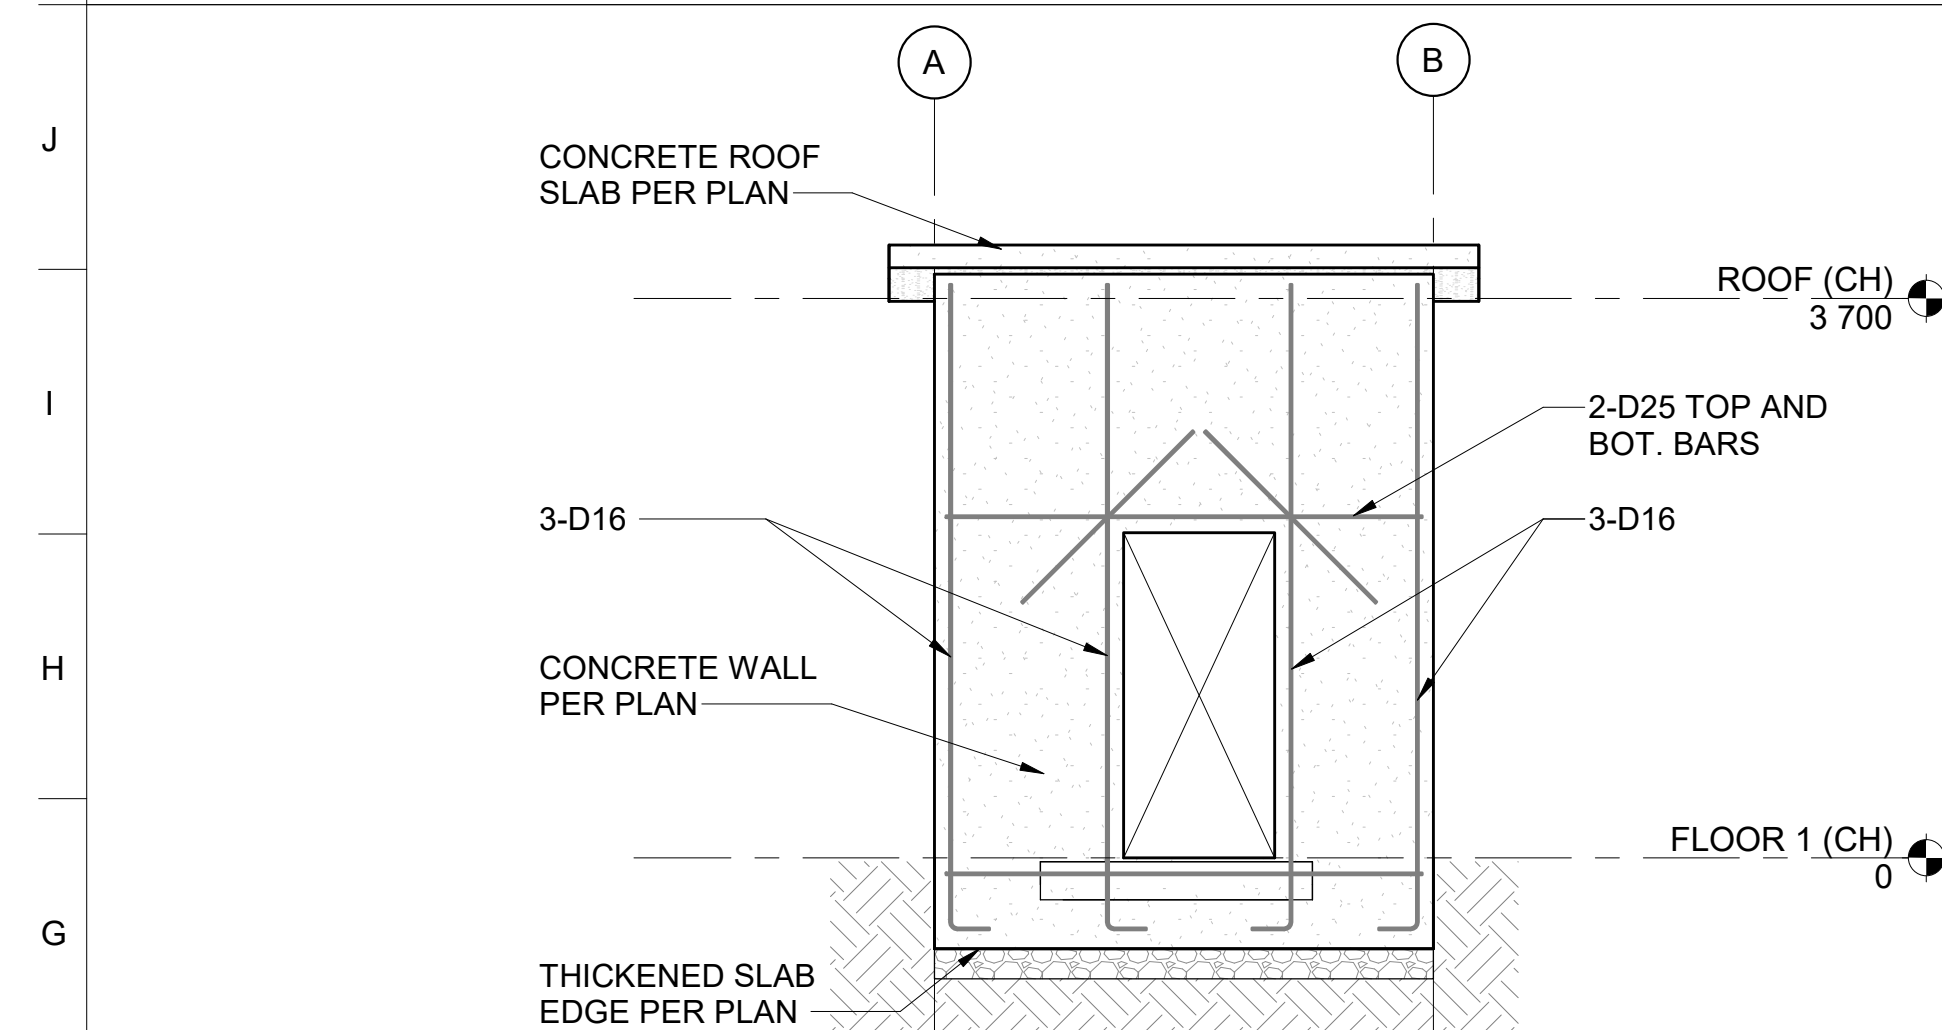


F1 CH - EXTERIOR ELEVATION - WEST (CLIN 0001)
SCALE 1 : 50

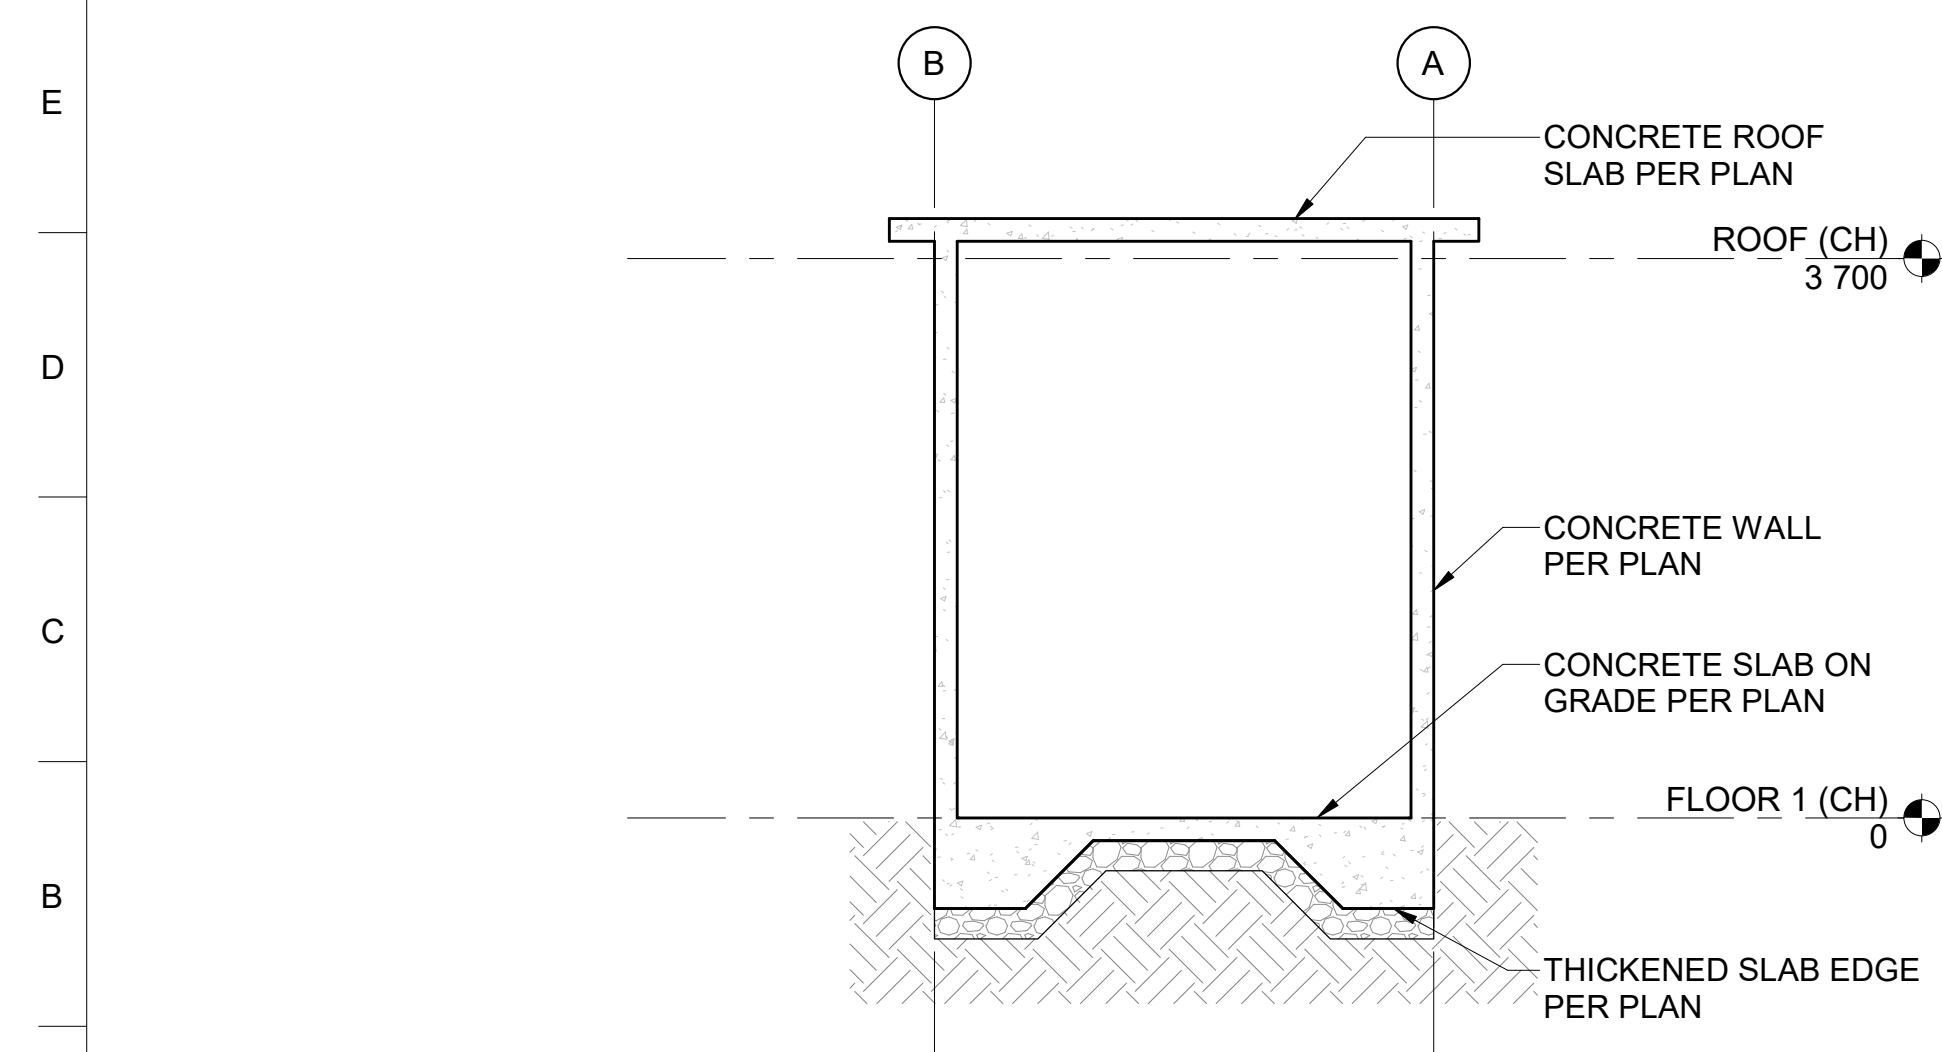


A1 CH - BUILDING SECTION (CLIN 0001)
SCALE 1 : 50

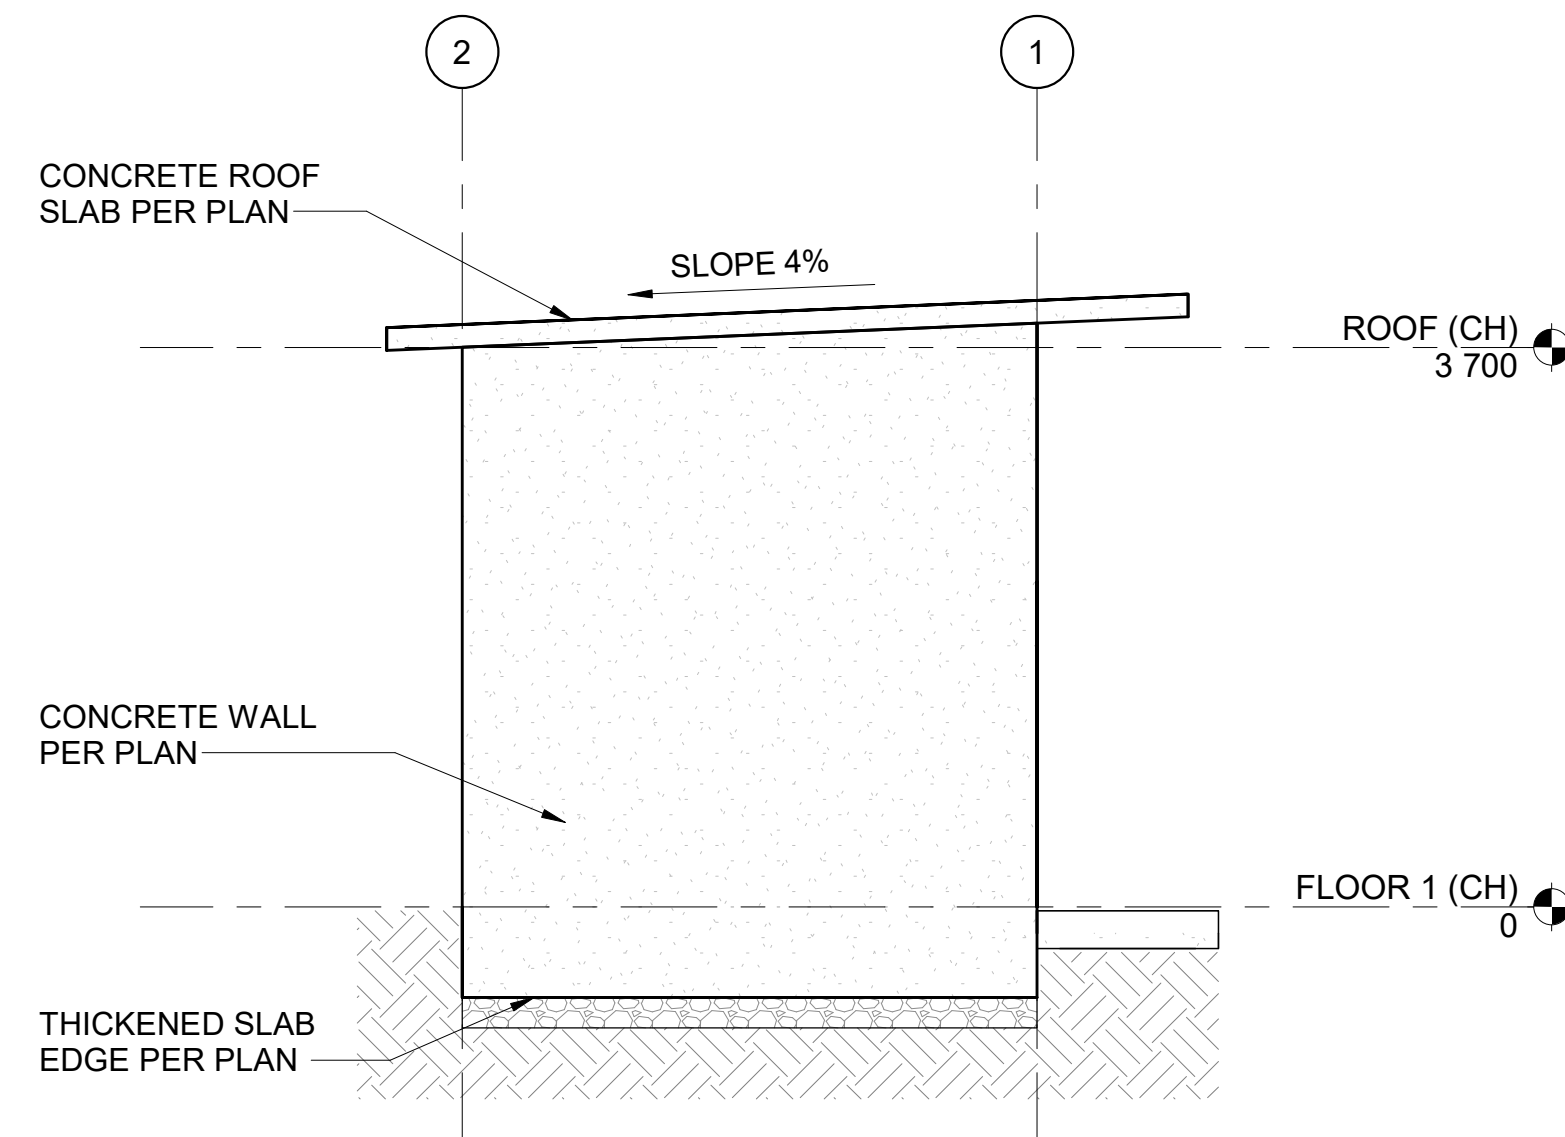

K12 CH - EXTERIOR ELEVATION - NORTH (CLIN 0001)
SCALE 1 : 50

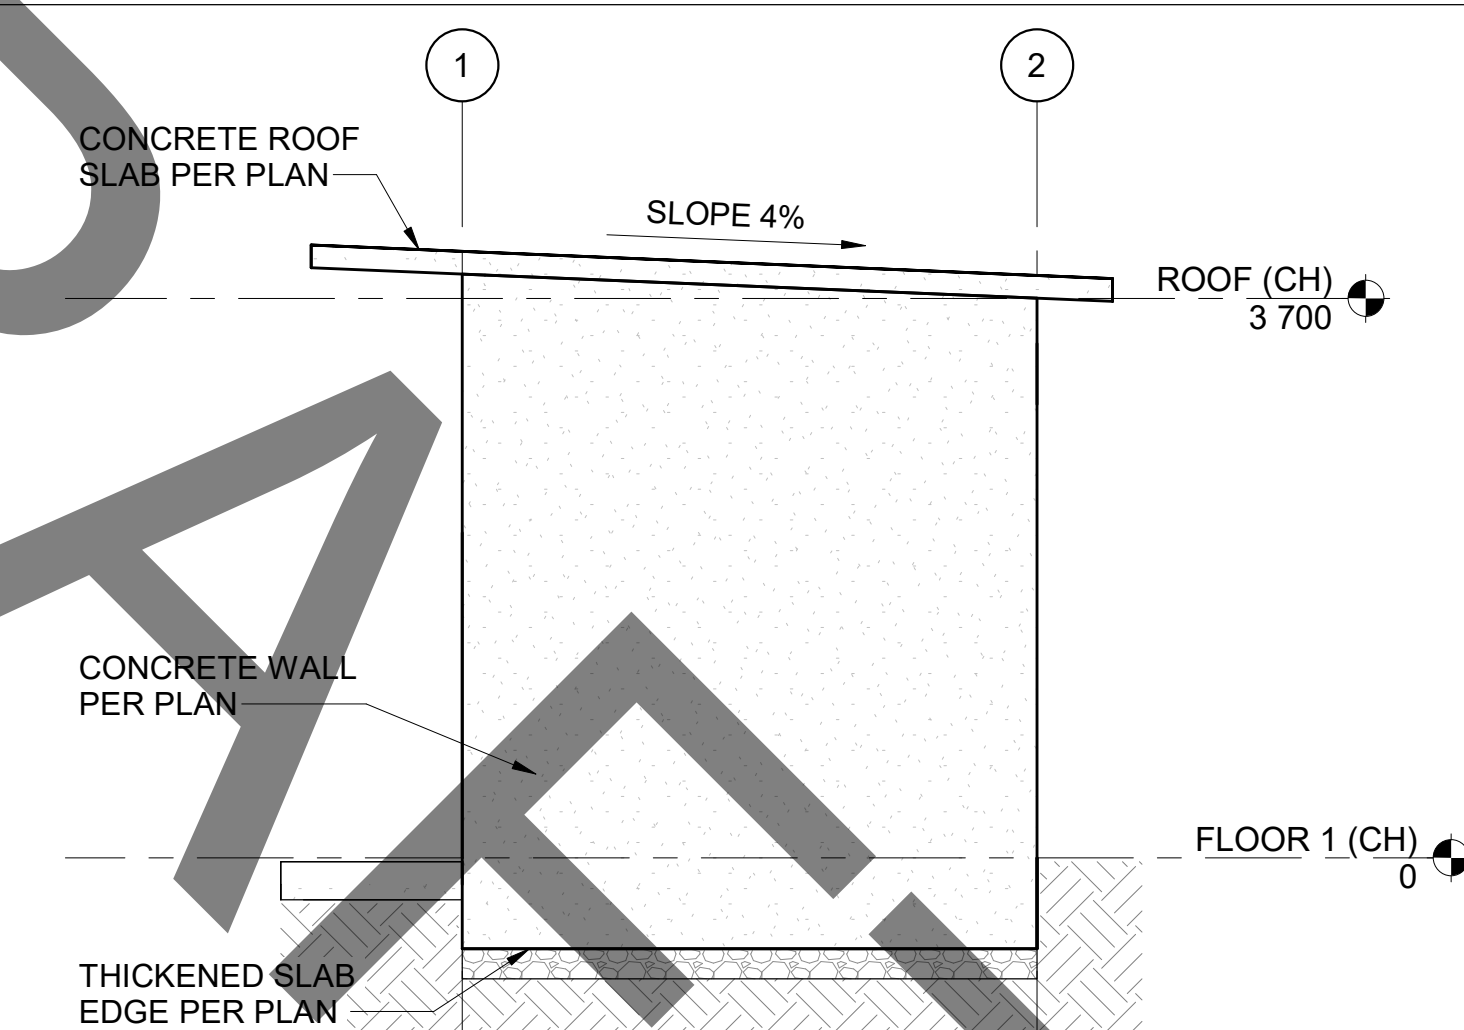


F12 CH - EXTERIOR ELEVATION - SOUTH (CLIN 0001)
SCALE 1 : 50

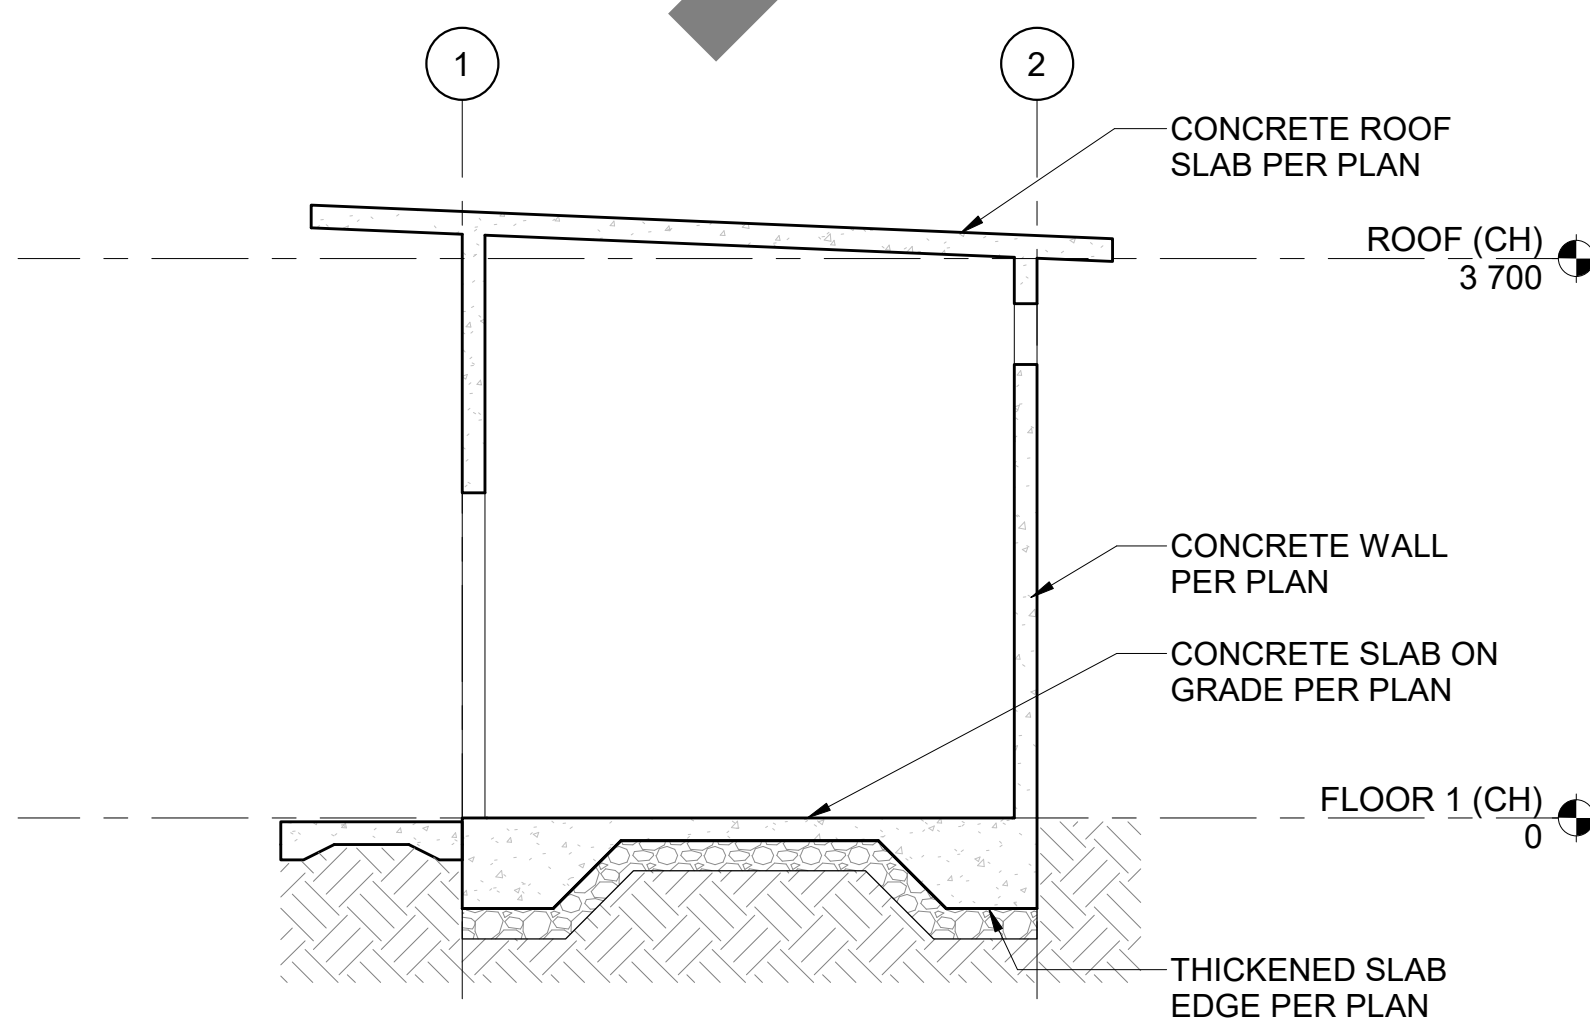

A12 CH - BUILDING SECTION (CLIN 0001)
SCALE 1 : 50

REFERENCE DRAWINGS

S-001 - GENERAL NOTES
S-002 - DESIGN DATA, DESIGN CODES AND STANDARDS,
ABBREVIATION
S-501 - TYPICAL REINFORCING STEEL DETAILS
S-502 - TYPICAL CONCRETE DETAILS
S-604 - CONCRETE FOOTING SCHEDULE
S-605 - CONCRETE WALL SCHEDULE

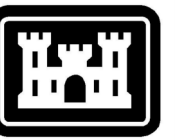

**US Army Corps
of Engineers ®**

[illegible]

NOTES

1. SEE ARCHITECTURAL DRAWINGS FOR DIMENSIONS, ELEVATIONS AND DETAILS NOT SHOWN ON STRUCTURAL DRAWINGS.
2. SEE ARCHITECTURAL DRAWINGS FOR FLOOR SLOPE.
3. VERIFY WITH ARCHITECT/MECHANICAL FOR SIZE AND LOCATION OF OPENINGS.

US ARMY CORPS OF ENGINEERS JAPAN ENGINEER DISTRICT ONJIMA WRECK OFFICE APO AP 96376-5132	ISSUED BY: A. PATEL	ISSUE DATE: JUNE 2018
 SSPM INTERNATIONAL, INC 501 KUNER STREET, SUITE 620 HONOLULU, HAWAII 96817	DRAWN BY: R. TANGONAN	SOLICITATION NO.:
	CHECKED BY: J. UNO	CONTRACT NO.:
	SUBMITTED BY: J. UNO	W912HN-17-D-0003
	SIZE:	
	AS/D	

Autodesk Docs://Vehicle Maint Shop Kadena/511758_TEMF_STRUC.MI

File Path:

Plot Date: 12/16/2025 3:37:42 PM

Plot Date:

CLIN 0001

GRAPHIC SCALE

GRAPHIC SCALE

SCALE: 1 : 50

0 1000 2000




ALL DIMENSIONS AND/OR DIMENSIONS SHOWN IN
CALLOUT/ NOTES ARE IN MILLIMETERS UNLESS
NOTED OTHERWISE.

FY20 MCA PN77833 VEHICLE MAINTENANCE SHOP
 CABLE HUT EXTERIOR ELEVATIONS AND
 BUILDING SECTIONS (CLIN 0001)


SHEET ID
CH
S-G102

INTERMEDIATE DESIGN

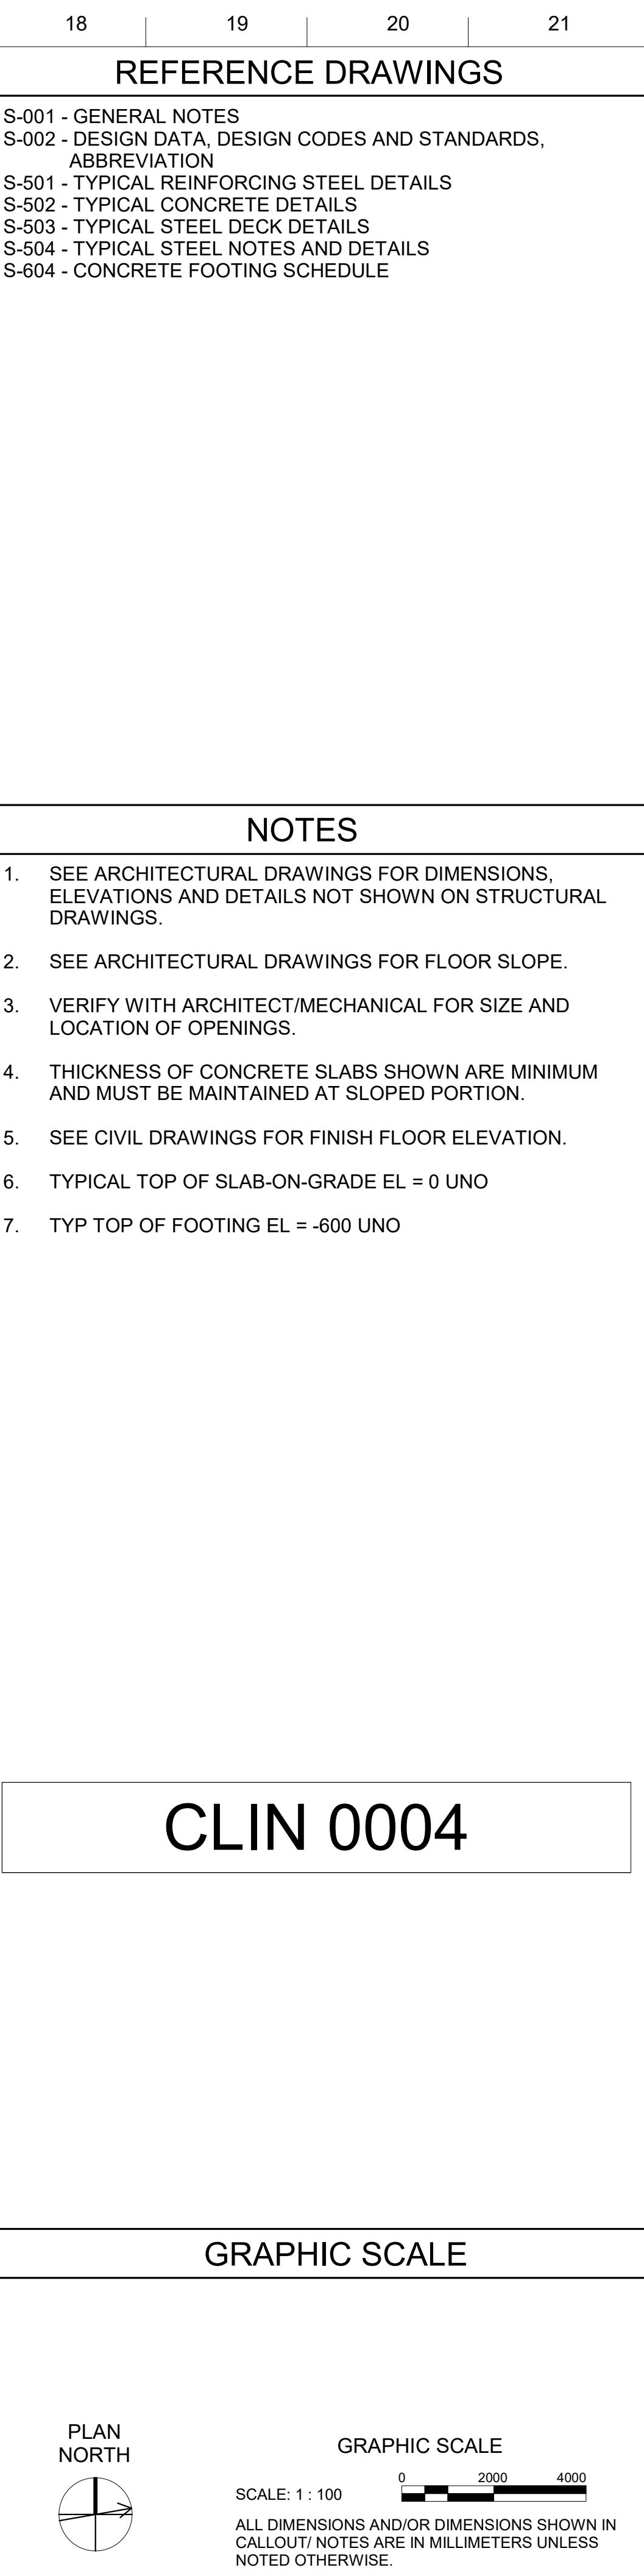[illegible]





ALL DIMENSIONS AND/OR DIMENSIONS SHOWN IN
CALLOUT/ NOTES ARE IN MILLIMETERS UNLESS
NOTED OTHERWISE.

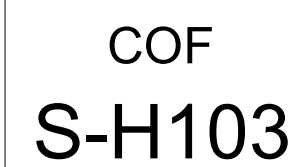

Plot Date: 12/16/2025 3:37:45 PM


Autodesk Docs://Vehicle Maint Shop Kadena/511758_TEMF_STRUC.M

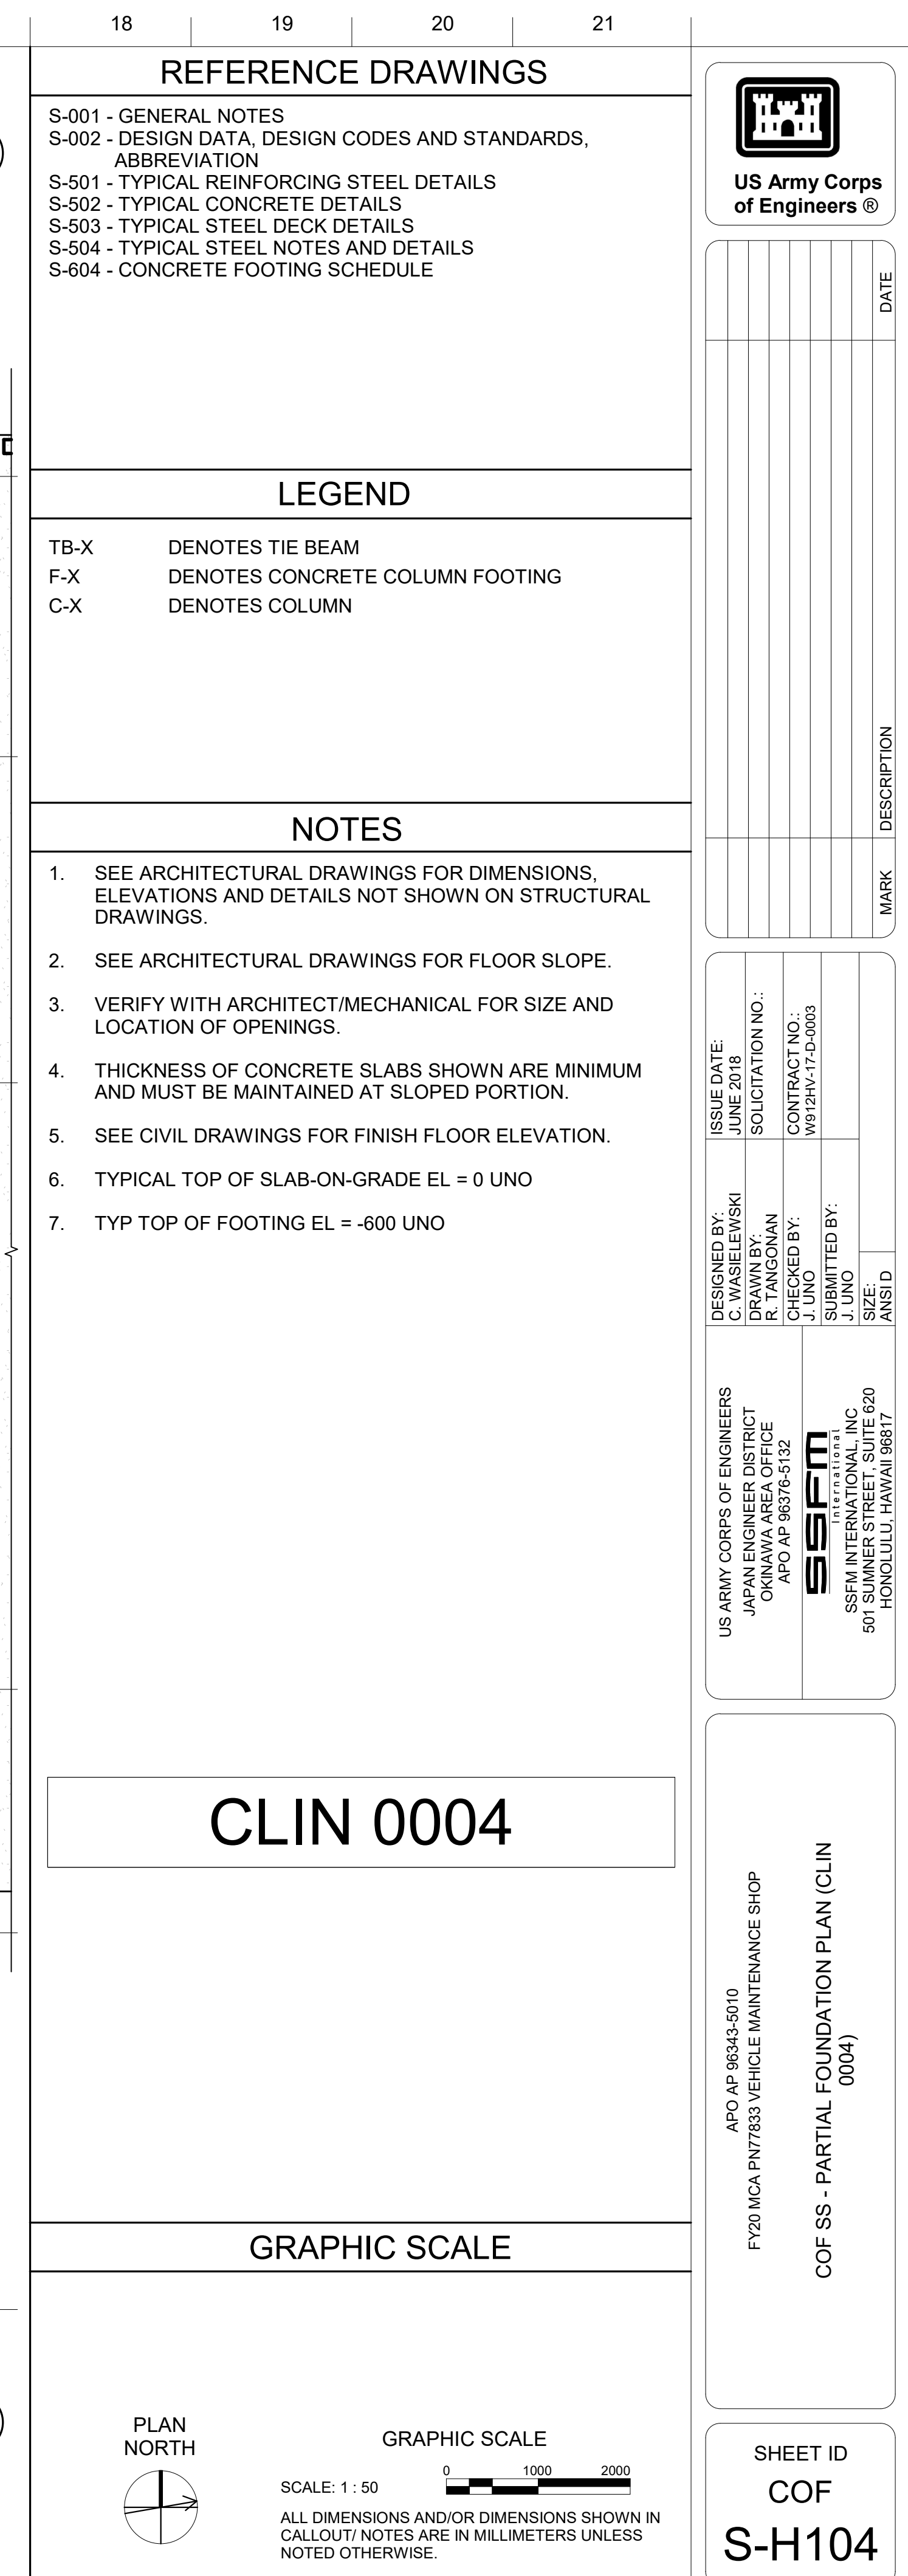

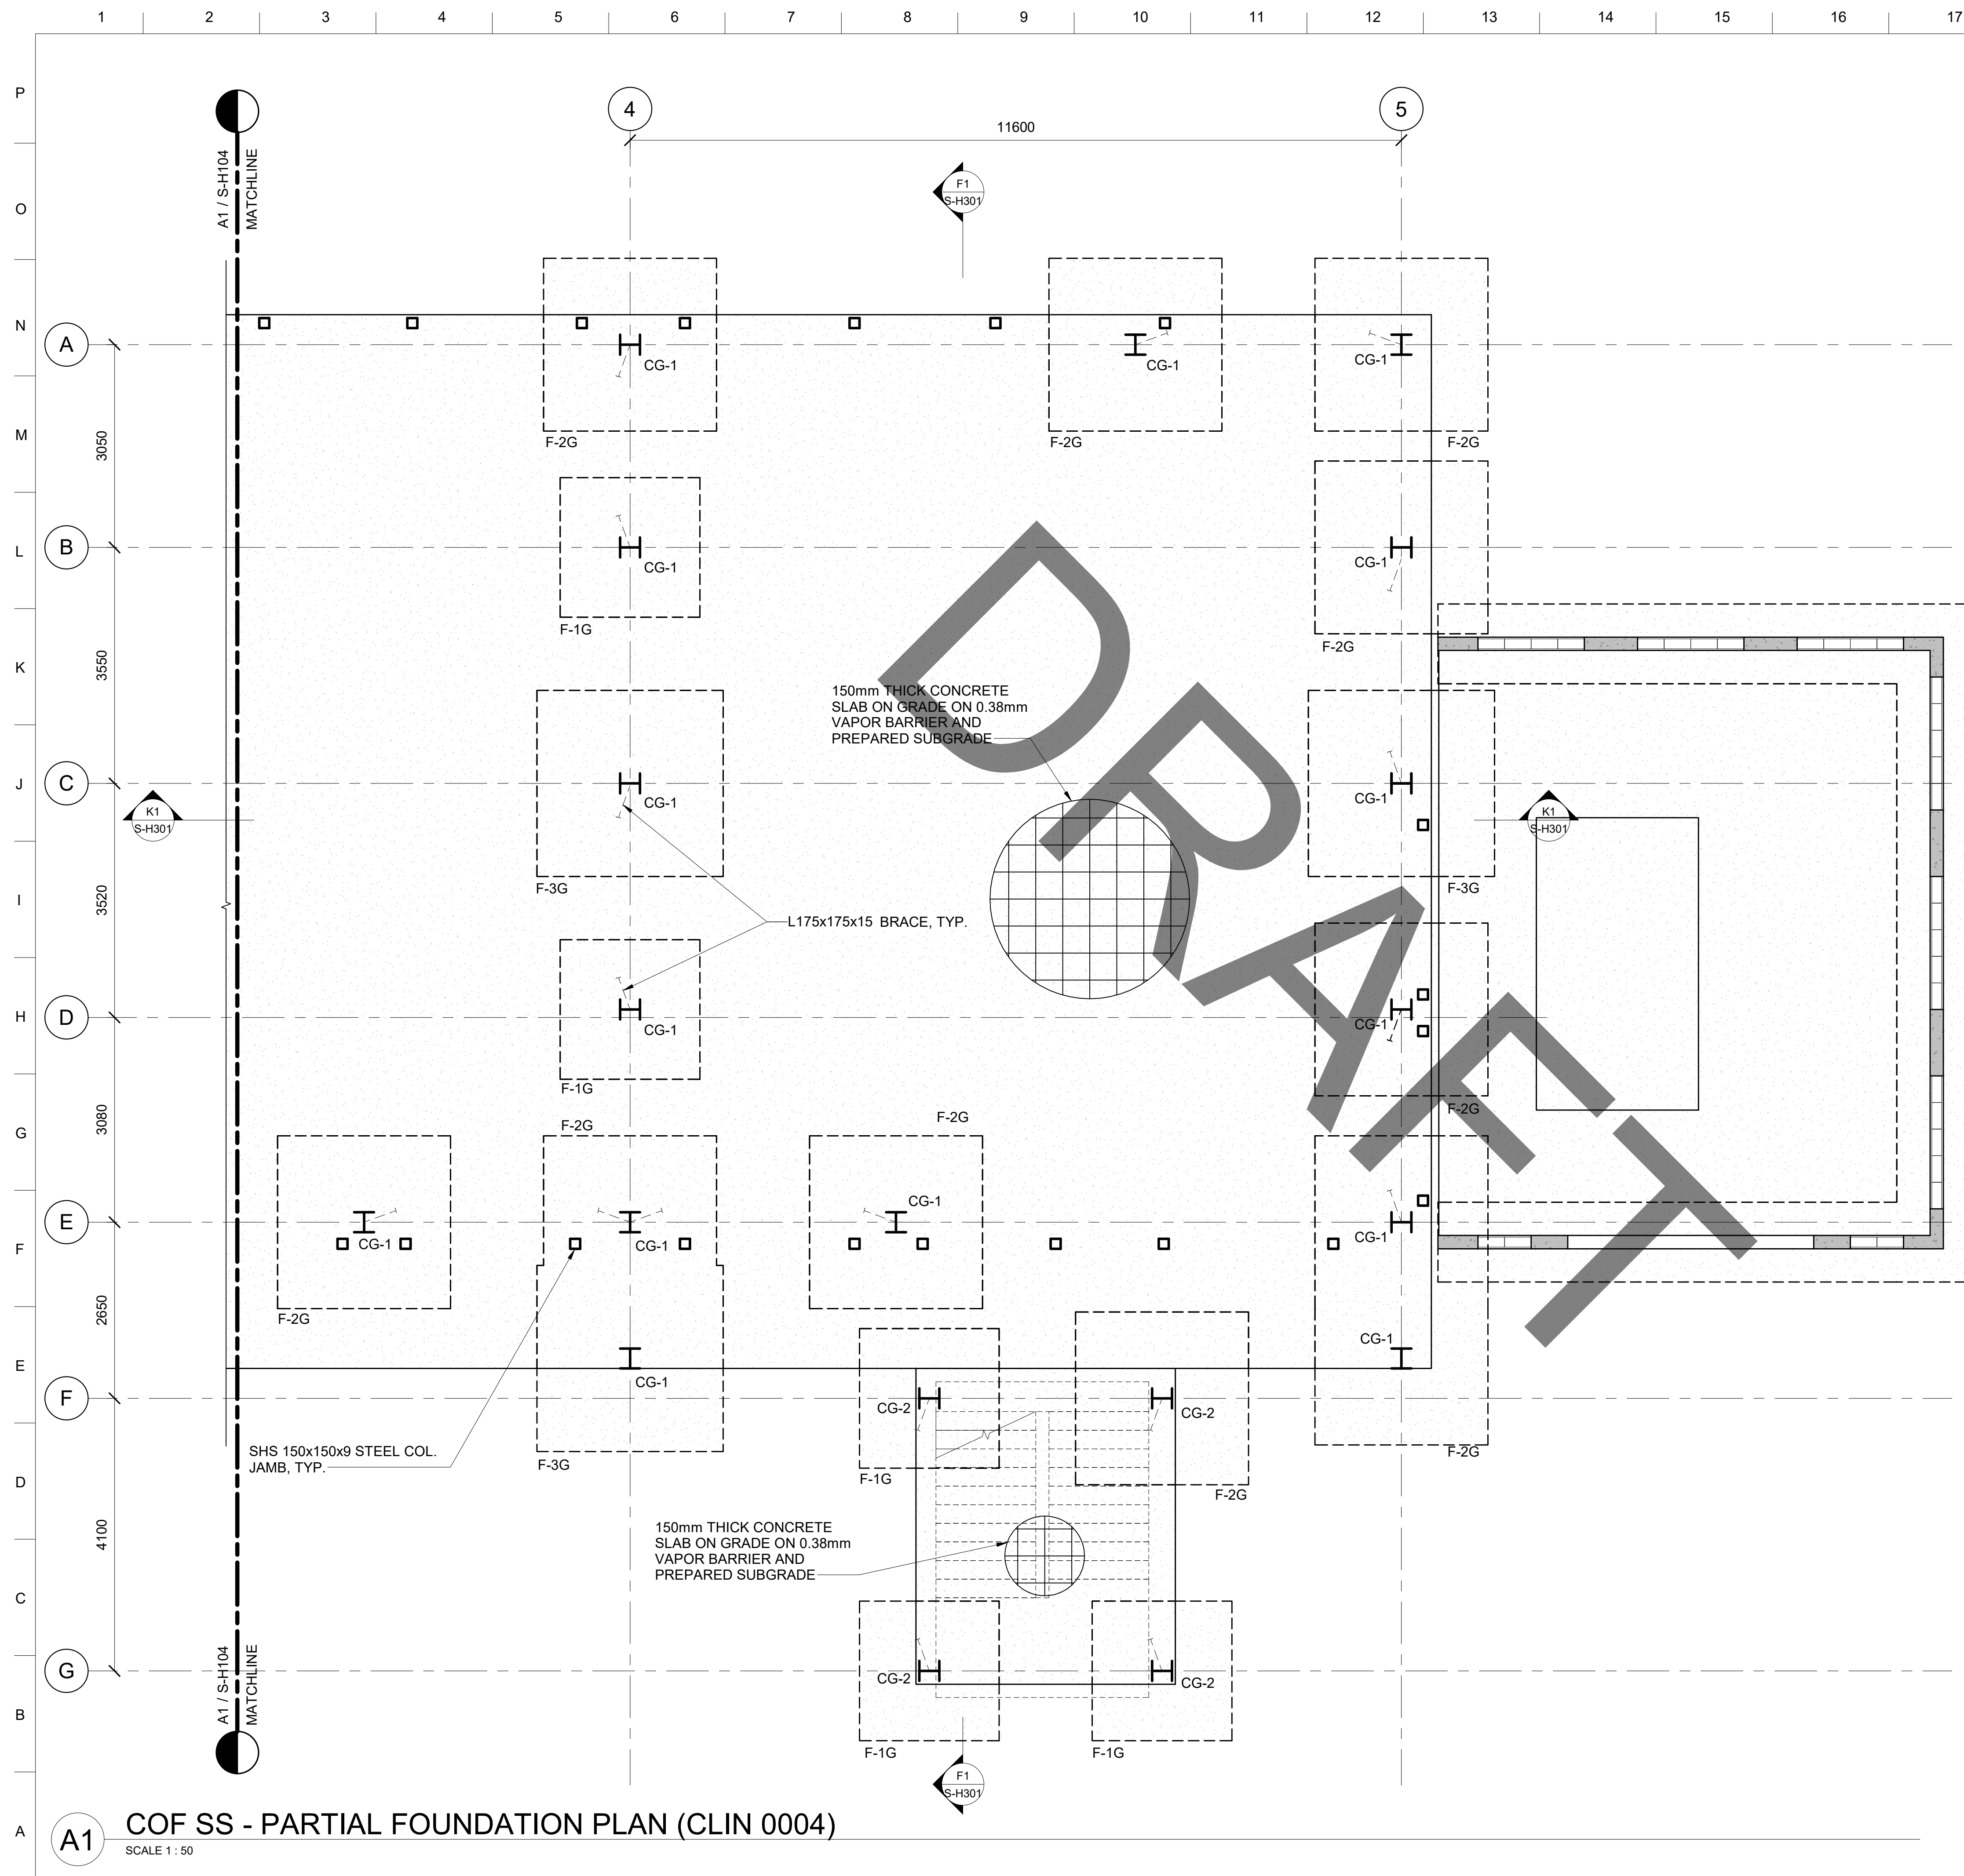

REFERENCE DRAWINGS

S-001 - GENERAL NOTES
S-002 - DESIGN DATA, DESIGN CODES AND STANDARDS,
ABBREVIATION
S-501 - TYPICAL REINFORCING STEEL DETAILS
S-502 - TYPICAL CONCRETE DETAILS
S-503 - TYPICAL STEEL DECK DETAILS
S-504 - TYPICAL STEEL NOTES AND DETAILS
S-604 - CONCRETE FOOTING SCHEDULE

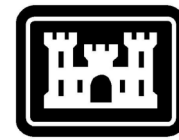

**US Army Corps
of Engineers®**

[illegible]

LEGEND

TB-X	DENOTES TIE BEAM
F-X	DENOTES CONCRETE COLUMN FOOTING
C-X	DENOTES COLUMN

NOTES

1. SEE ARCHITECTURAL DRAWINGS FOR DIMENSIONS, ELEVATIONS AND DETAILS NOT SHOWN ON STRUCTURAL DRAWINGS.
2. SEE ARCHITECTURAL DRAWINGS FOR FLOOR SLOPE.
3. VERIFY WITH ARCHITECT/MECHANICAL FOR SIZE AND LOCATION OF OPENINGS.
4. THICKNESS OF CONCRETE SLABS SHOWN ARE MINIMUM AND MUST BE MAINTAINED AT SLOPED PORTION.
5. SEE CIVIL DRAWINGS FOR FINISH FLOOR ELEVATION.
6. TYPICAL TOP OF SLAB-ON-GRADE EL = 0 UNO
7. TYP TOP OF FOOTING EL = -600 UNO

US ARMY CORPS OF ENGINEERS JAPAN ENGINEER DISTRICT OKINAWA AREA OFFICE APO AF 96376-5132		ISSUED DATE: JUNE 1981	
DESIGNED BY: C. WASIELEWSKI		SOLICITATION NO.: W912HV-17-D-0003	
CHECKED BY: R. TANGOMAN		CONTRACT NO.: W912HV-17-D-0003	
QUANTITY: 1 UNIT		ISSUED BY: J. UNO	
SSFM INTERNATIONAL INC. 501 SUMNER STREET, SUITE 620 HONOLULU, HAWAII 96817		SIZE: A4	

Plot Date: 12/16/2025 3:37:47 PM
File Path: Autodesk Docs://Vehicle Maint Shop/Kadena/511759_TEMF_STRUC.rvt

CLIN 0004

GRAPHIC SCALE

PLAN
NORTH

GRAPHIC SCALE


SCALE: 1 : 50


ALL DIMENSIONS AND/OR DIMENSIONS SHOWN IN
CALLOUT/ NOTES ARE IN MILLIMETERS UNLESS
NOTED OTHERWISE.


SHEET ID

COF
S-H105


INTERMEDIATE DESIGN

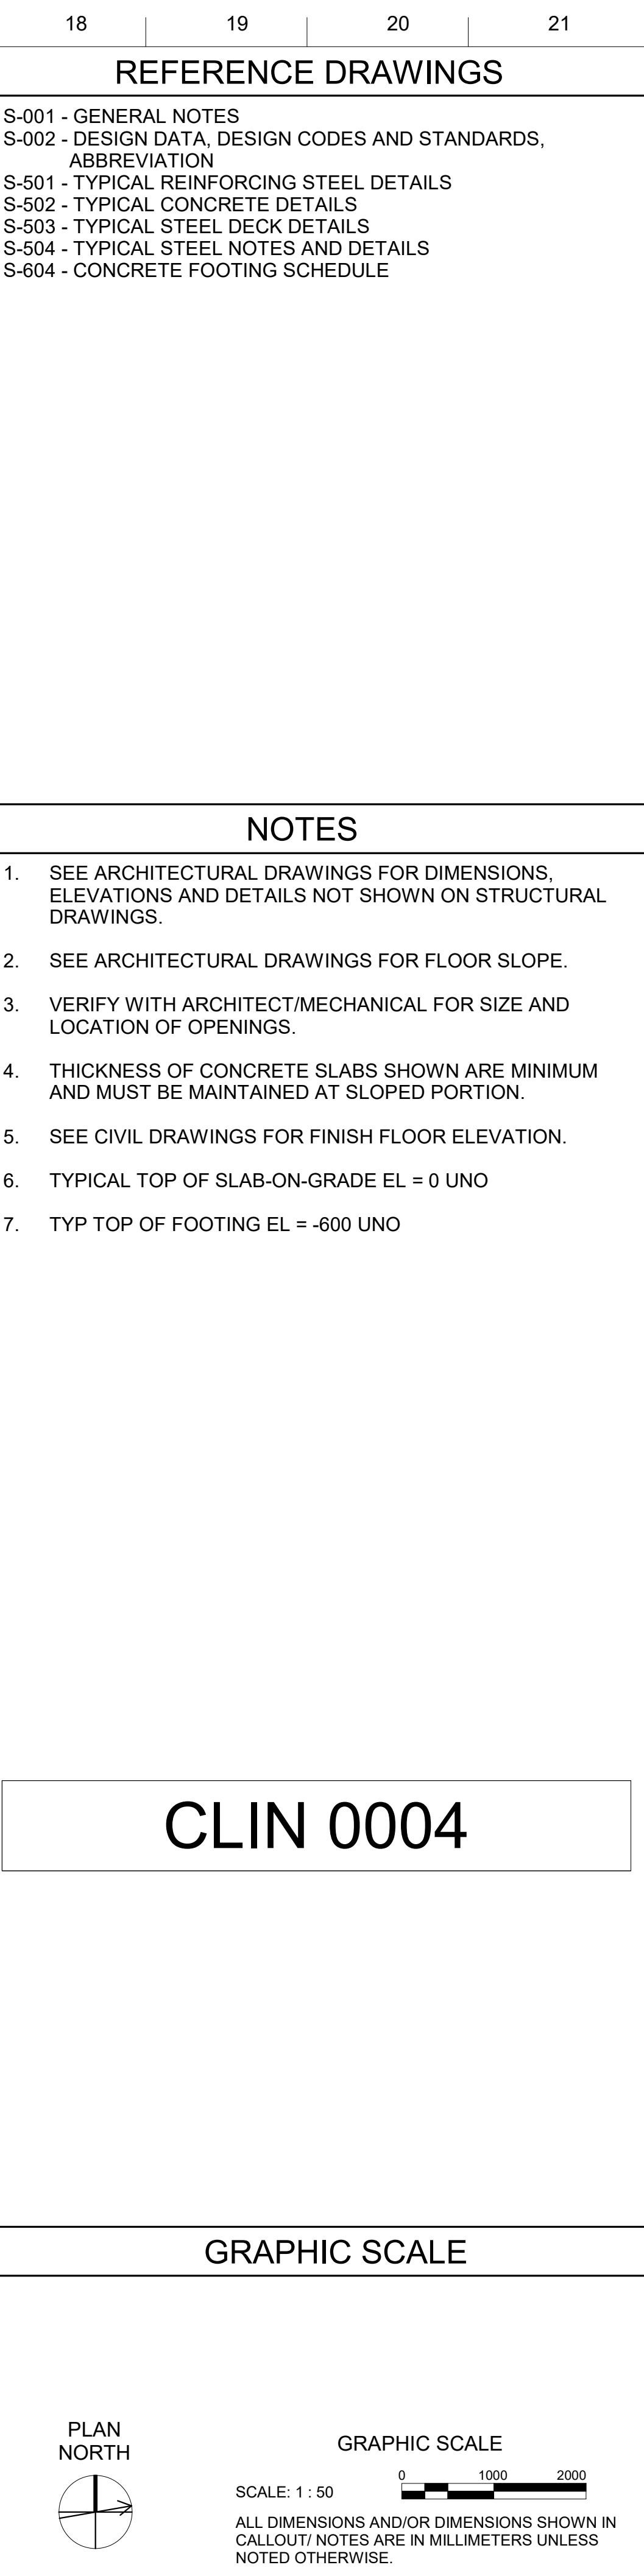

 
 US Army Corps of Engineers®		MARK DESCRIPTION DATE	
DESIGNED BY: C. WASELEWSKI JAPAN ENGINEER DISTRICT R. TANGONAN		ISSUE DATE: JUNE 2018 SOLICITATION NO.: W912HV-17-D-0003	
CHECKED BY: J. UNO		CONTRACT NO.: W912HV-17-D-0003	
SUBMITTED BY: J. UNO		J. UNO	
US ARMY CORPS OF ENGINEERS JAPAN ENGINEER DISTRICT OKINAWA AREA OFFICE APO AP 96376-5132		SSFm SSFm INTERNATIONAL, INC. 501 SUMNER STREET, SUITE 620 HONOLULU, HAWAII 96817	

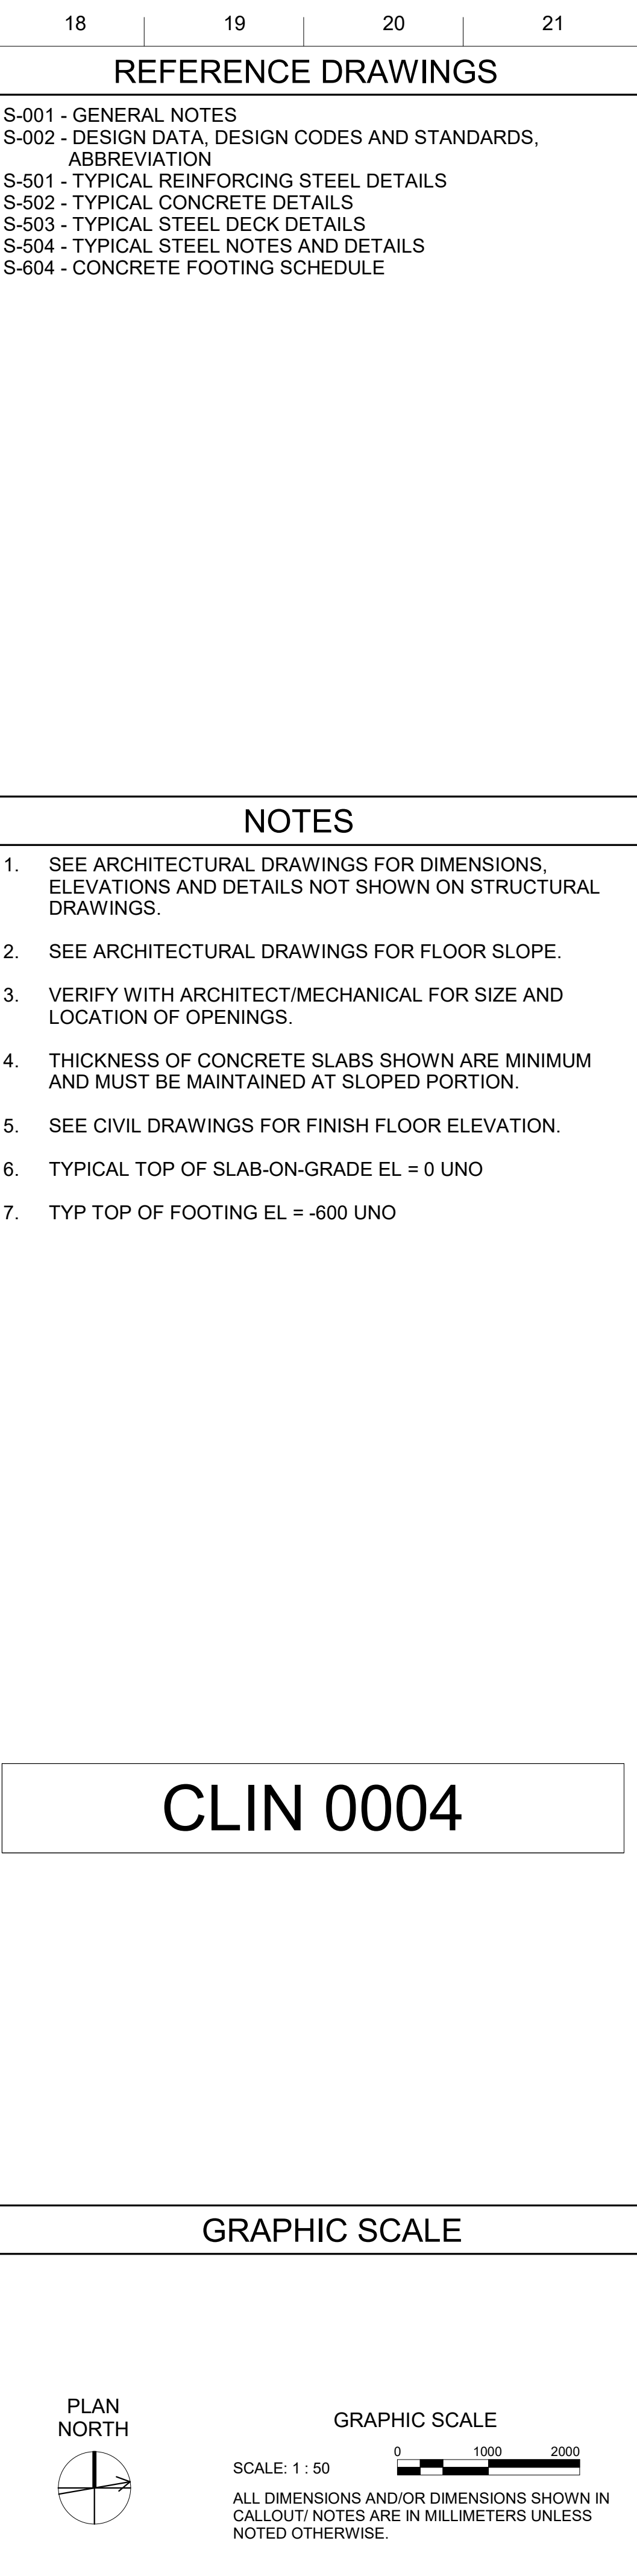


NTERMEDIATE DESIGN
 Plot Date: 12/16/2025 3:37:53 PM
 File Path: AutodesK Docs\\Vehicle Maint Shop\\Kodama\\11759_TEMI_STRUC.NT

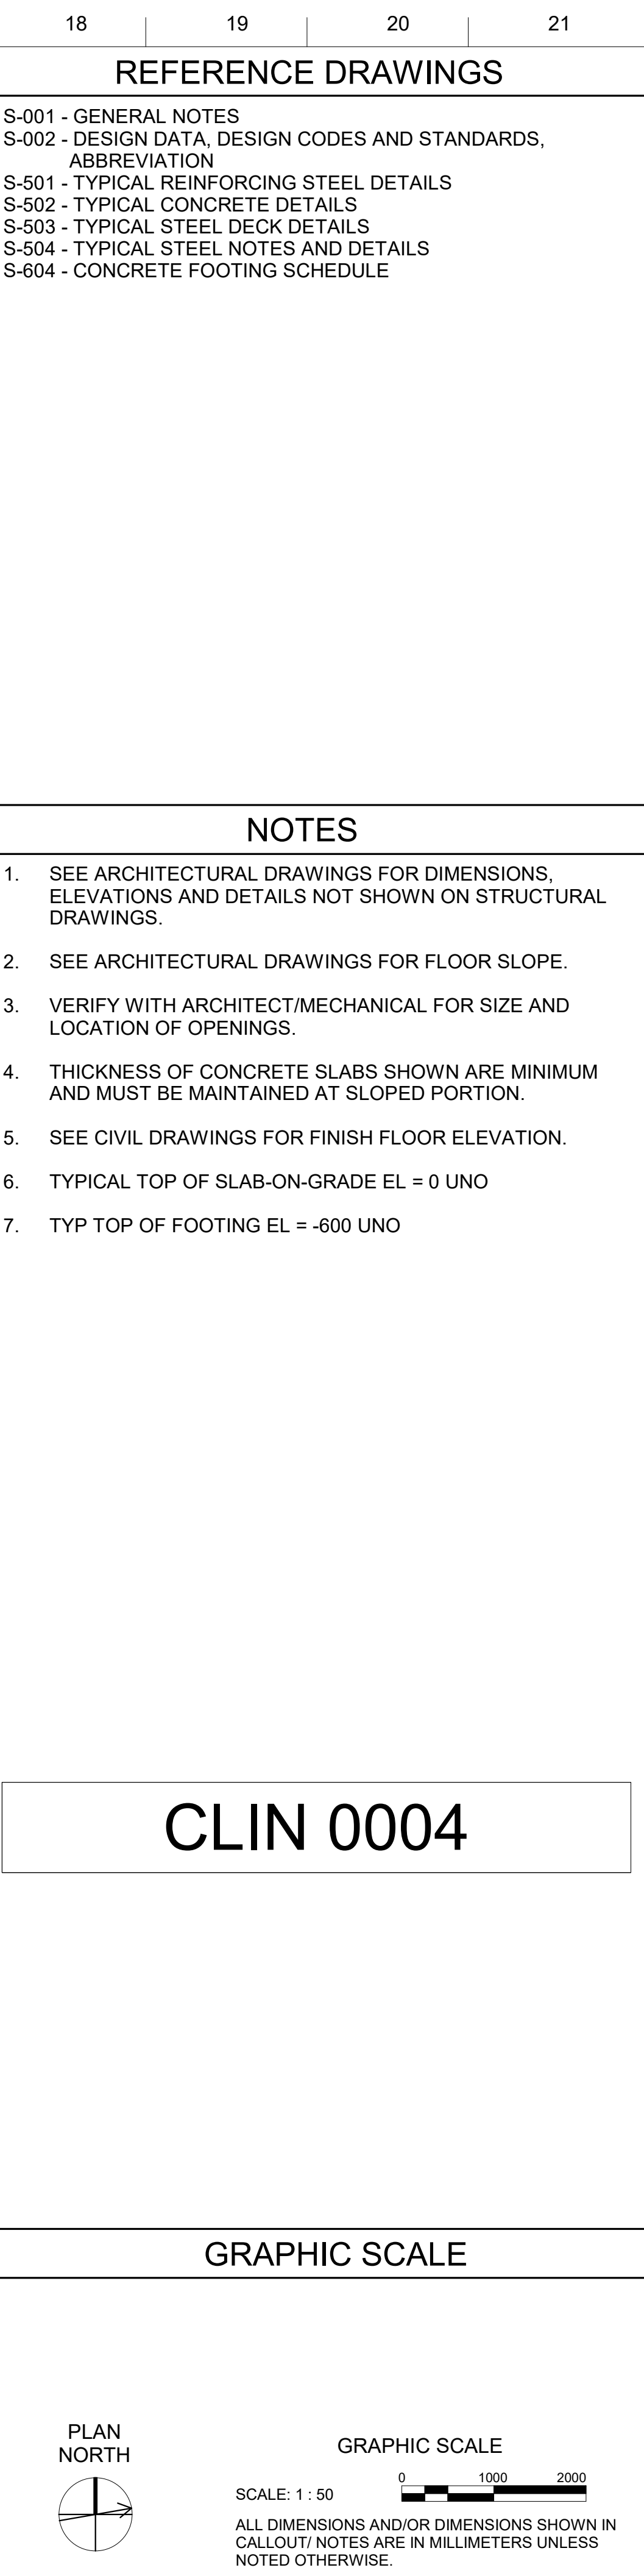


SHEET ID		COF	
S-H108			
COF SS - PARTIAL ROOF FLOOR FRAMING PLAN (CLIN 0004)			
F220 MCA PN7833 VEHICLE MAINTENANCE SHOP			
APO AP 96343-5010			
US ARMY CORPS OF ENGINEERS			
JAPAN ENGINEER DISTRICT			
OKINAWA AREA OFFICE			
APO AP 96376-5132			
DESIGNED BY:		ISSUE DATE:	
C. WASELEWSKI		JUNE 2018	
SOLICITATION NO.:			
R. TANGONAN			
CHECKED BY:		CONTRACT NO.:	
J. UNO		WB12HV-17-D-0003	
J. UNO			
ANSI D		MARK	
SIZE:		DESCRIPTION	
SSFM INTERIOR COATING, INC.			
501 SUMNER STREET, SUITE 620			
HONOLULU, HAWAII 96817			

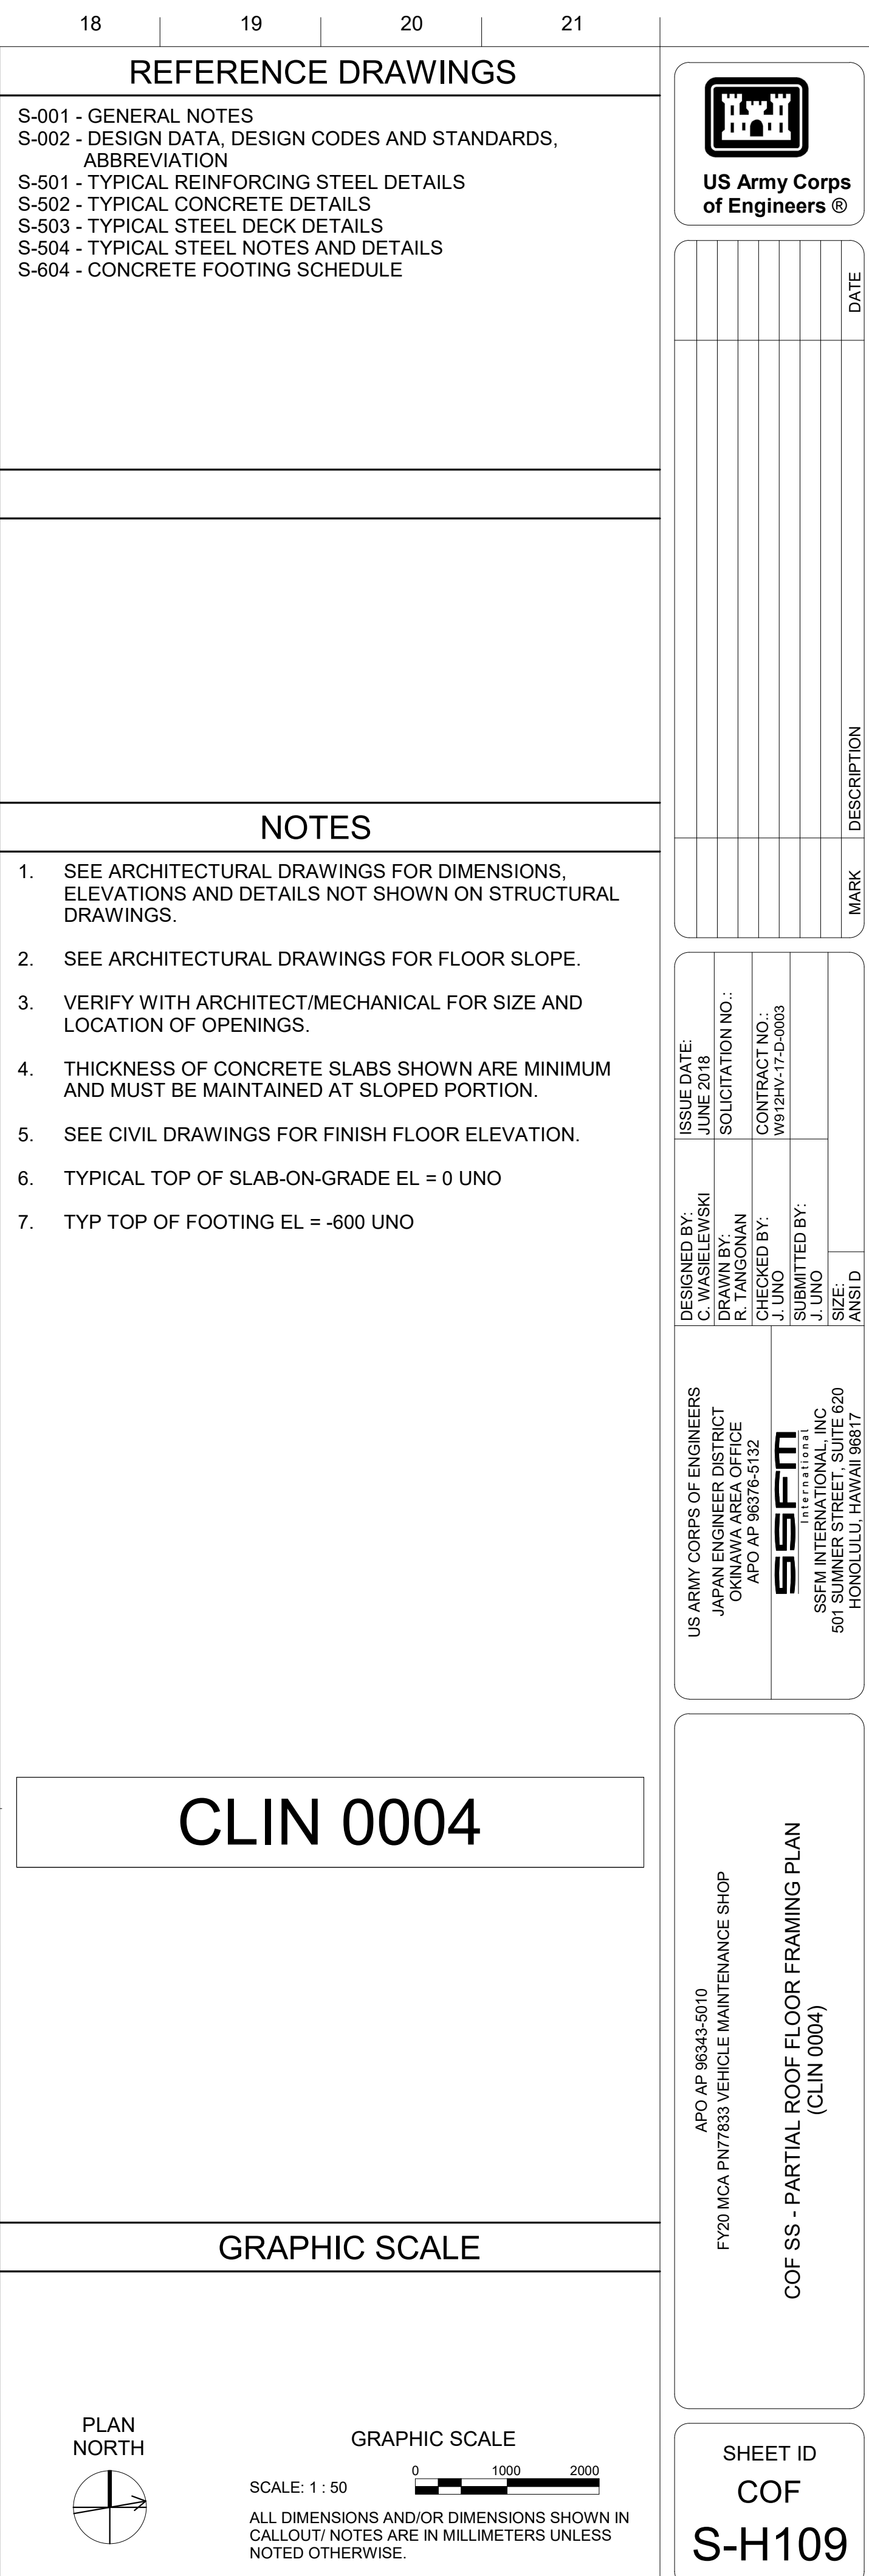


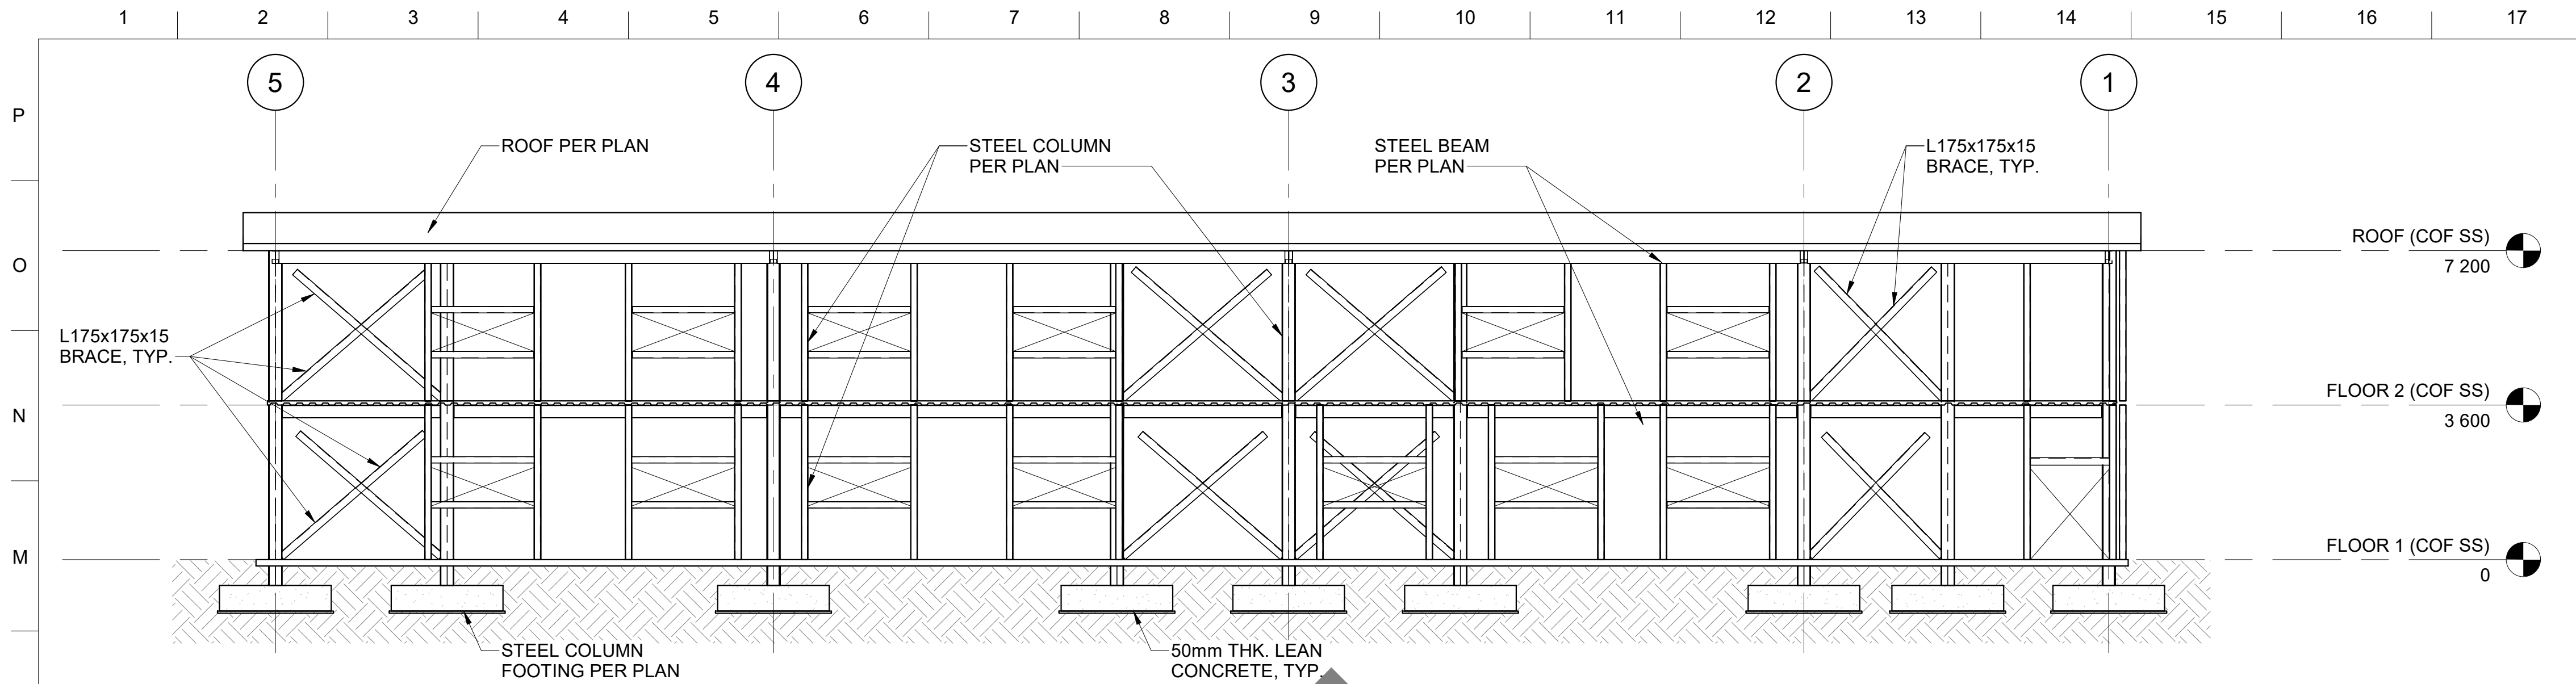


L1 COF SS - EXTERIOR ELEVATION NORTH (CLIN 0004)
SCALE 1 : 100

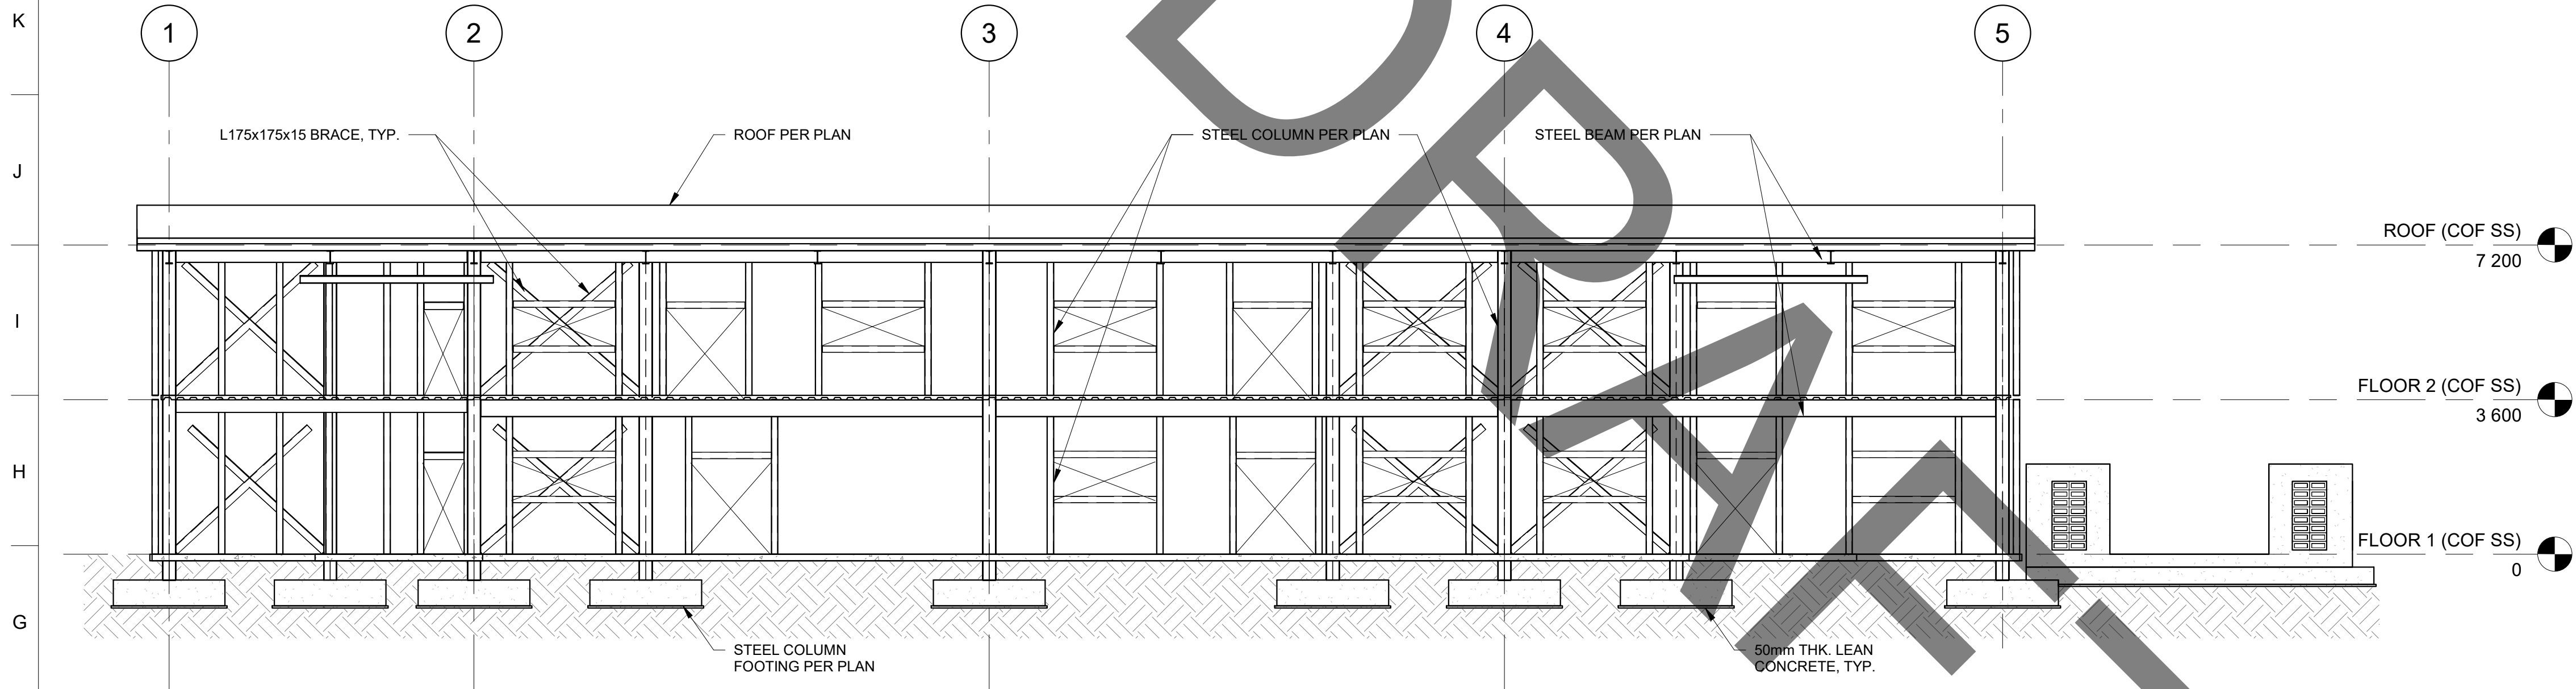

F1 COF SS - EXTERIOR ELEVATION SOUTH (CLIN 0004)
SCALE 1 : 100

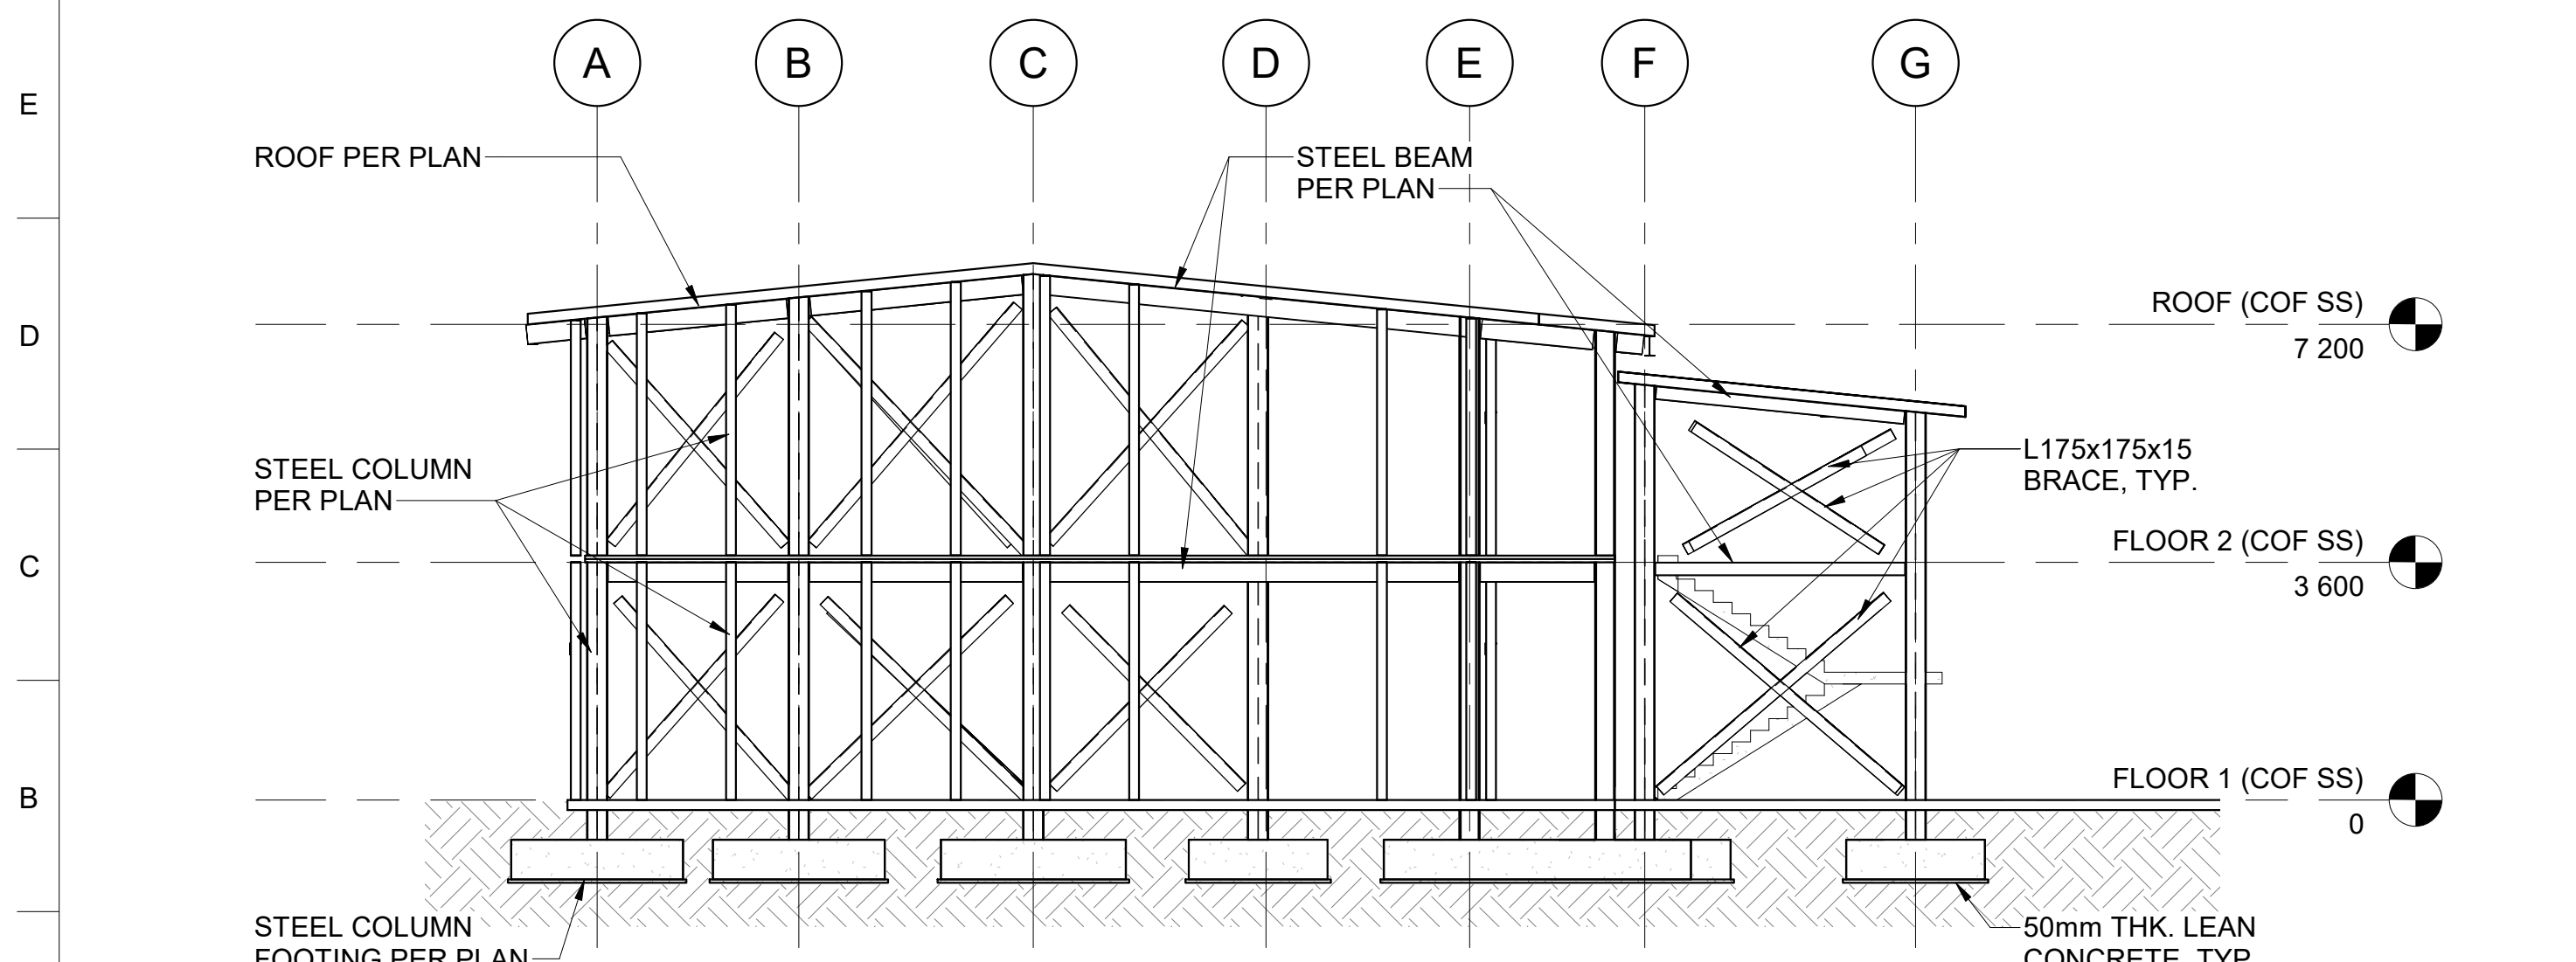

A1 COF SS - EXTERIOR ELEVATION WEST (CLIN 0004)
SCALE 1 : 100

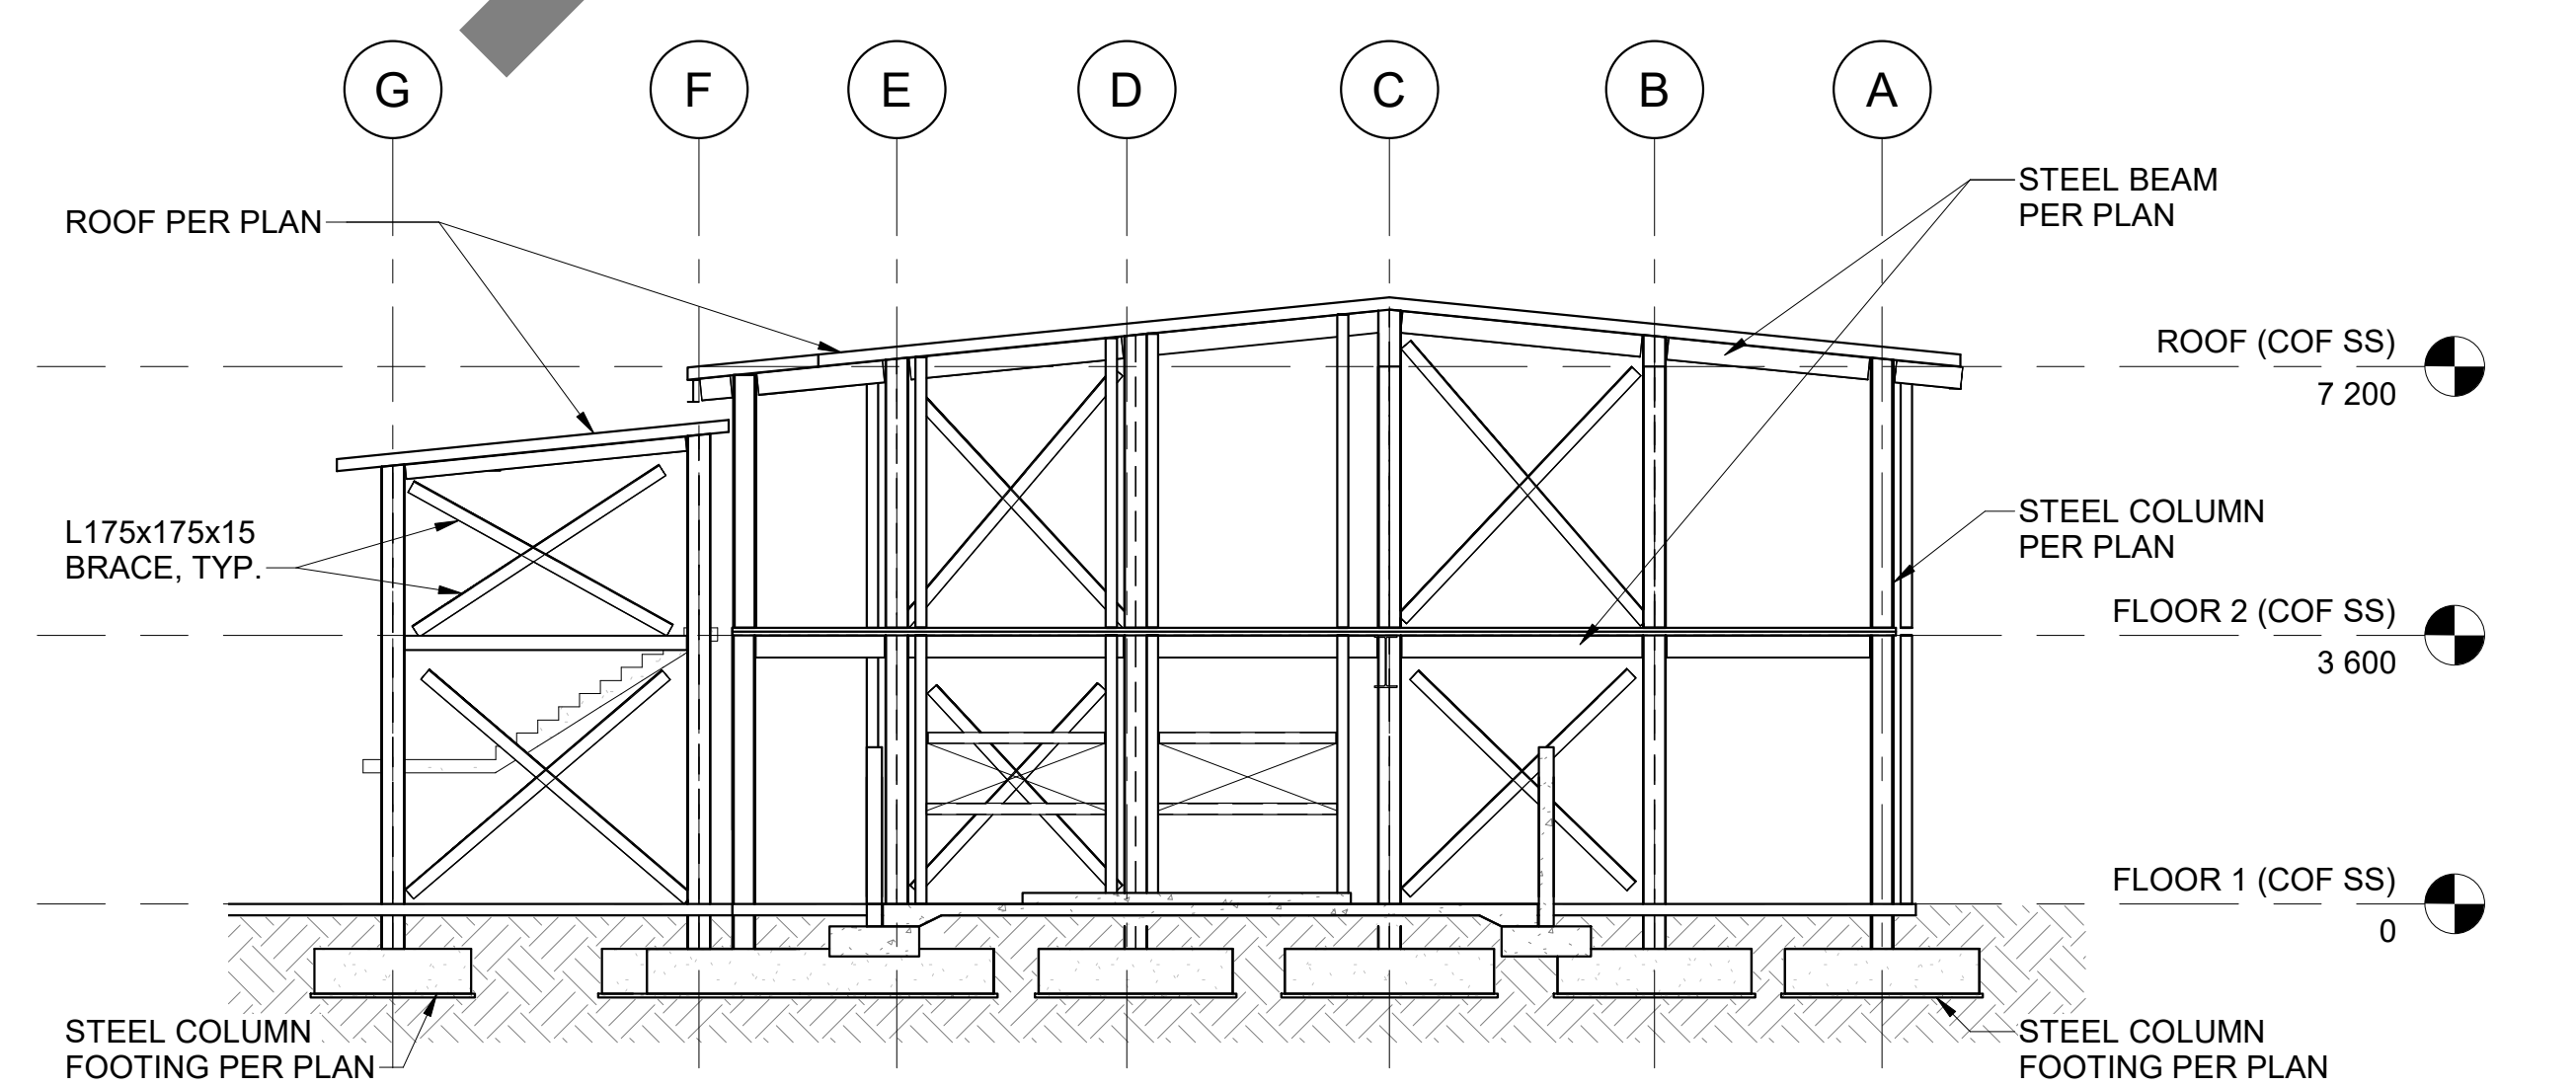

A12 COF SS - EXTERIOR ELEVATION EAST (CLIN 0004)
SCALE 1 : 100

REFERENCE DRAWINGS


- S-001 - GENERAL NOTES
- S-002 - DESIGN DATA, DESIGN CODES AND STANDARDS, ABBREVIATION
- S-501 - TYPICAL REINFORCING STEEL DETAILS
- S-502 - TYPICAL CONCRETE DETAILS
- S-503 - TYPICAL STEEL DECK DETAILS
- S-504 - TYPICAL STEEL NOTES AND DETAILS
- S-604 - CONCRETE FOOTING SCHEDULE

NOTES

- SEE ARCHITECTURAL DRAWINGS FOR DIMENSIONS, ELEVATIONS AND DETAILS NOT SHOWN ON STRUCTURAL DRAWINGS.
- SEE ARCHITECTURAL DRAWINGS FOR FLOOR SLOPE.
- VERIFY WITH ARCHITECT/MECHANICAL FOR SIZE AND LOCATION OF OPENINGS.

CLIN 0004

GRAPHIC SCALE

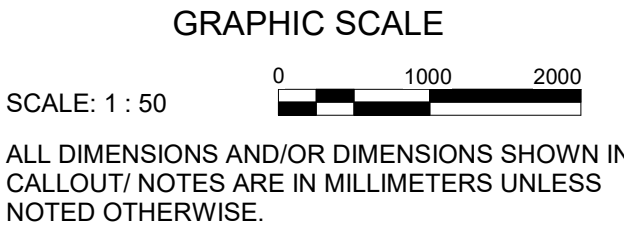

US Army Corps
of Engineers ®


MARK	DESCRIPTION	DATE

ISSUE DATE: JUNE 2018	SOLICITATION NO.: 	CONTRACT NO.: W72MY-17-D-0003
DESIGNED BY: C. WASIELEWSKI	DRAWN BY: R. TANGONAN	CHECKED BY: J. LINO


US ARMY CORPS OF ENGINEERS JAPAN ENGINEER DISTRICT OKINAWA AREA OFFICE APO AP 96316-5132	SSFM STRUCTURAL STEEL FABRICATING METHOD 501 SUMNER STREET, SUITE 620 HONOLULU, HAWAII 96817
---	---

APC AP 96343-5010 FY20 MCA PN77833 VEHICLE MAINTENANCE SHOP	COF SS - EXTERIOR ELEVATION (CLIN 0004)
--	---


SHEET ID COF S-H201

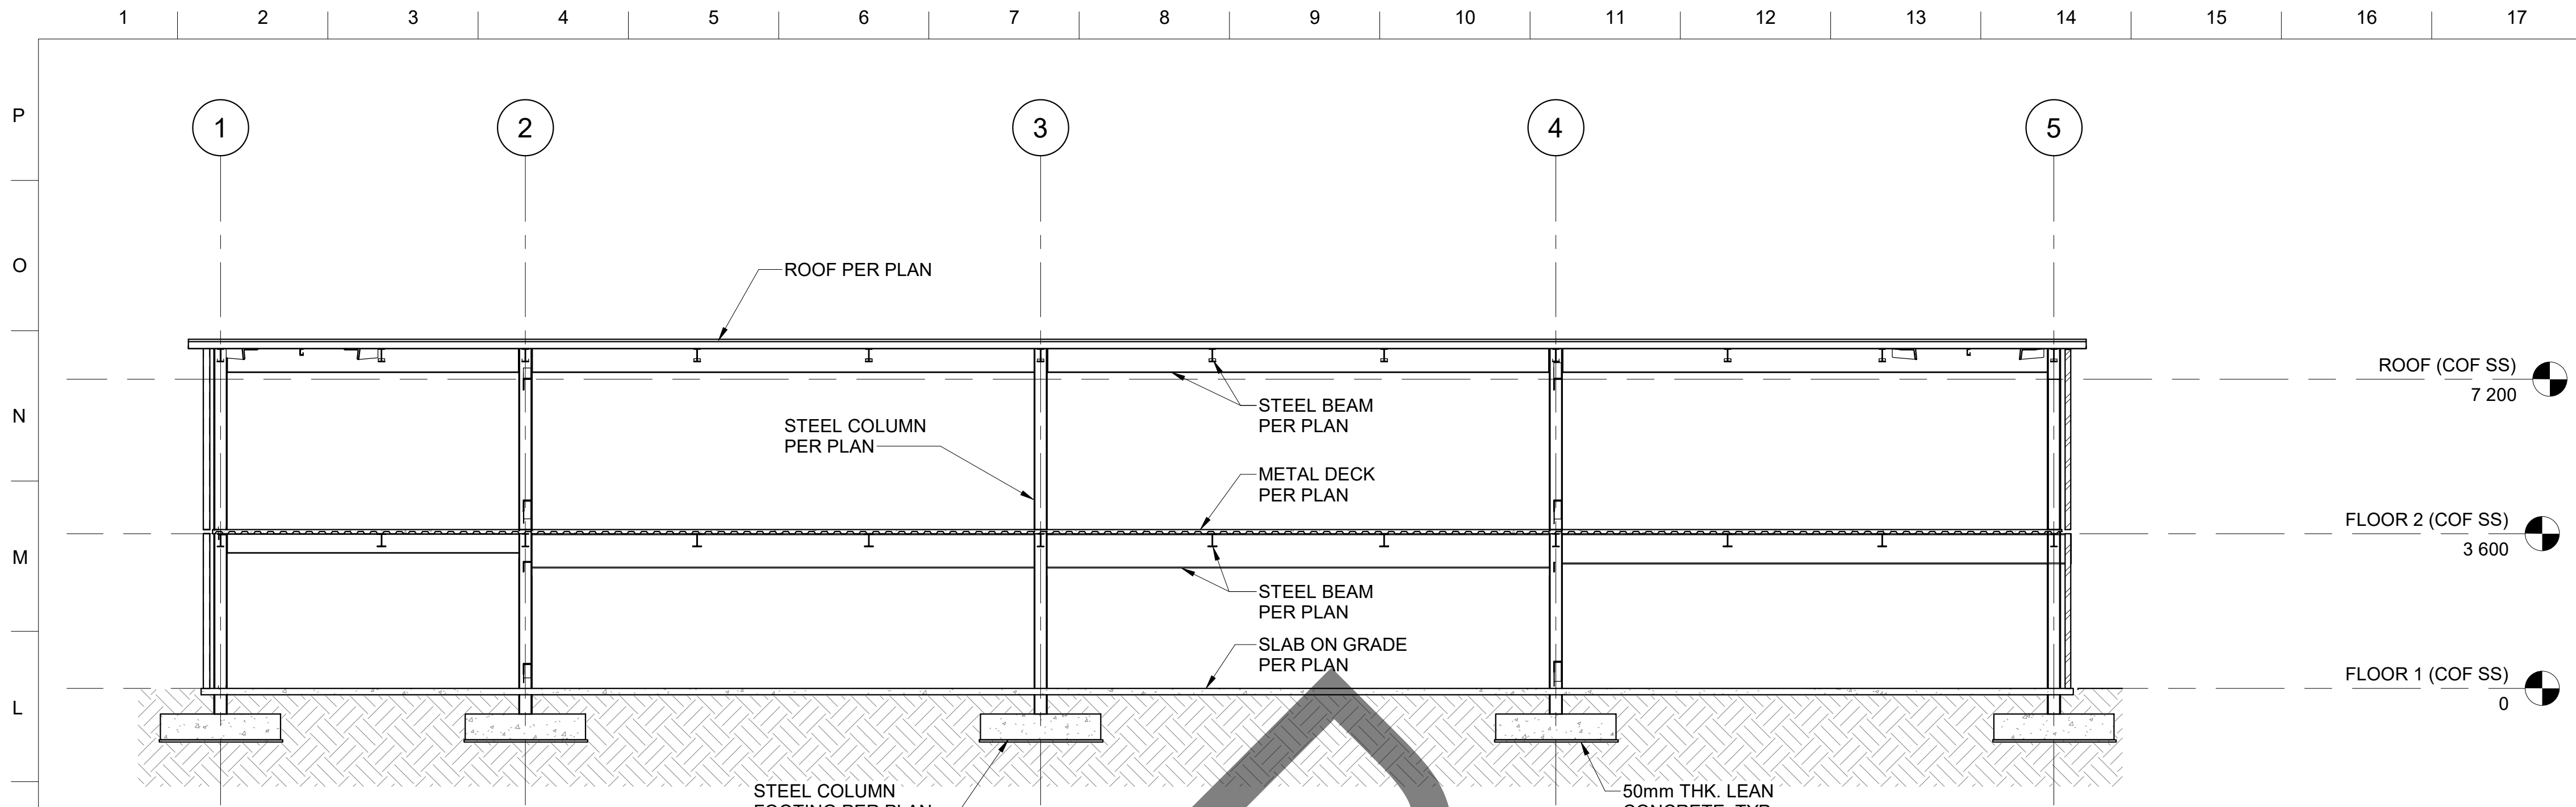


K1 COF SS - BUILDING SECTIONS (CLIN 0004)
SCALE 1 : 100

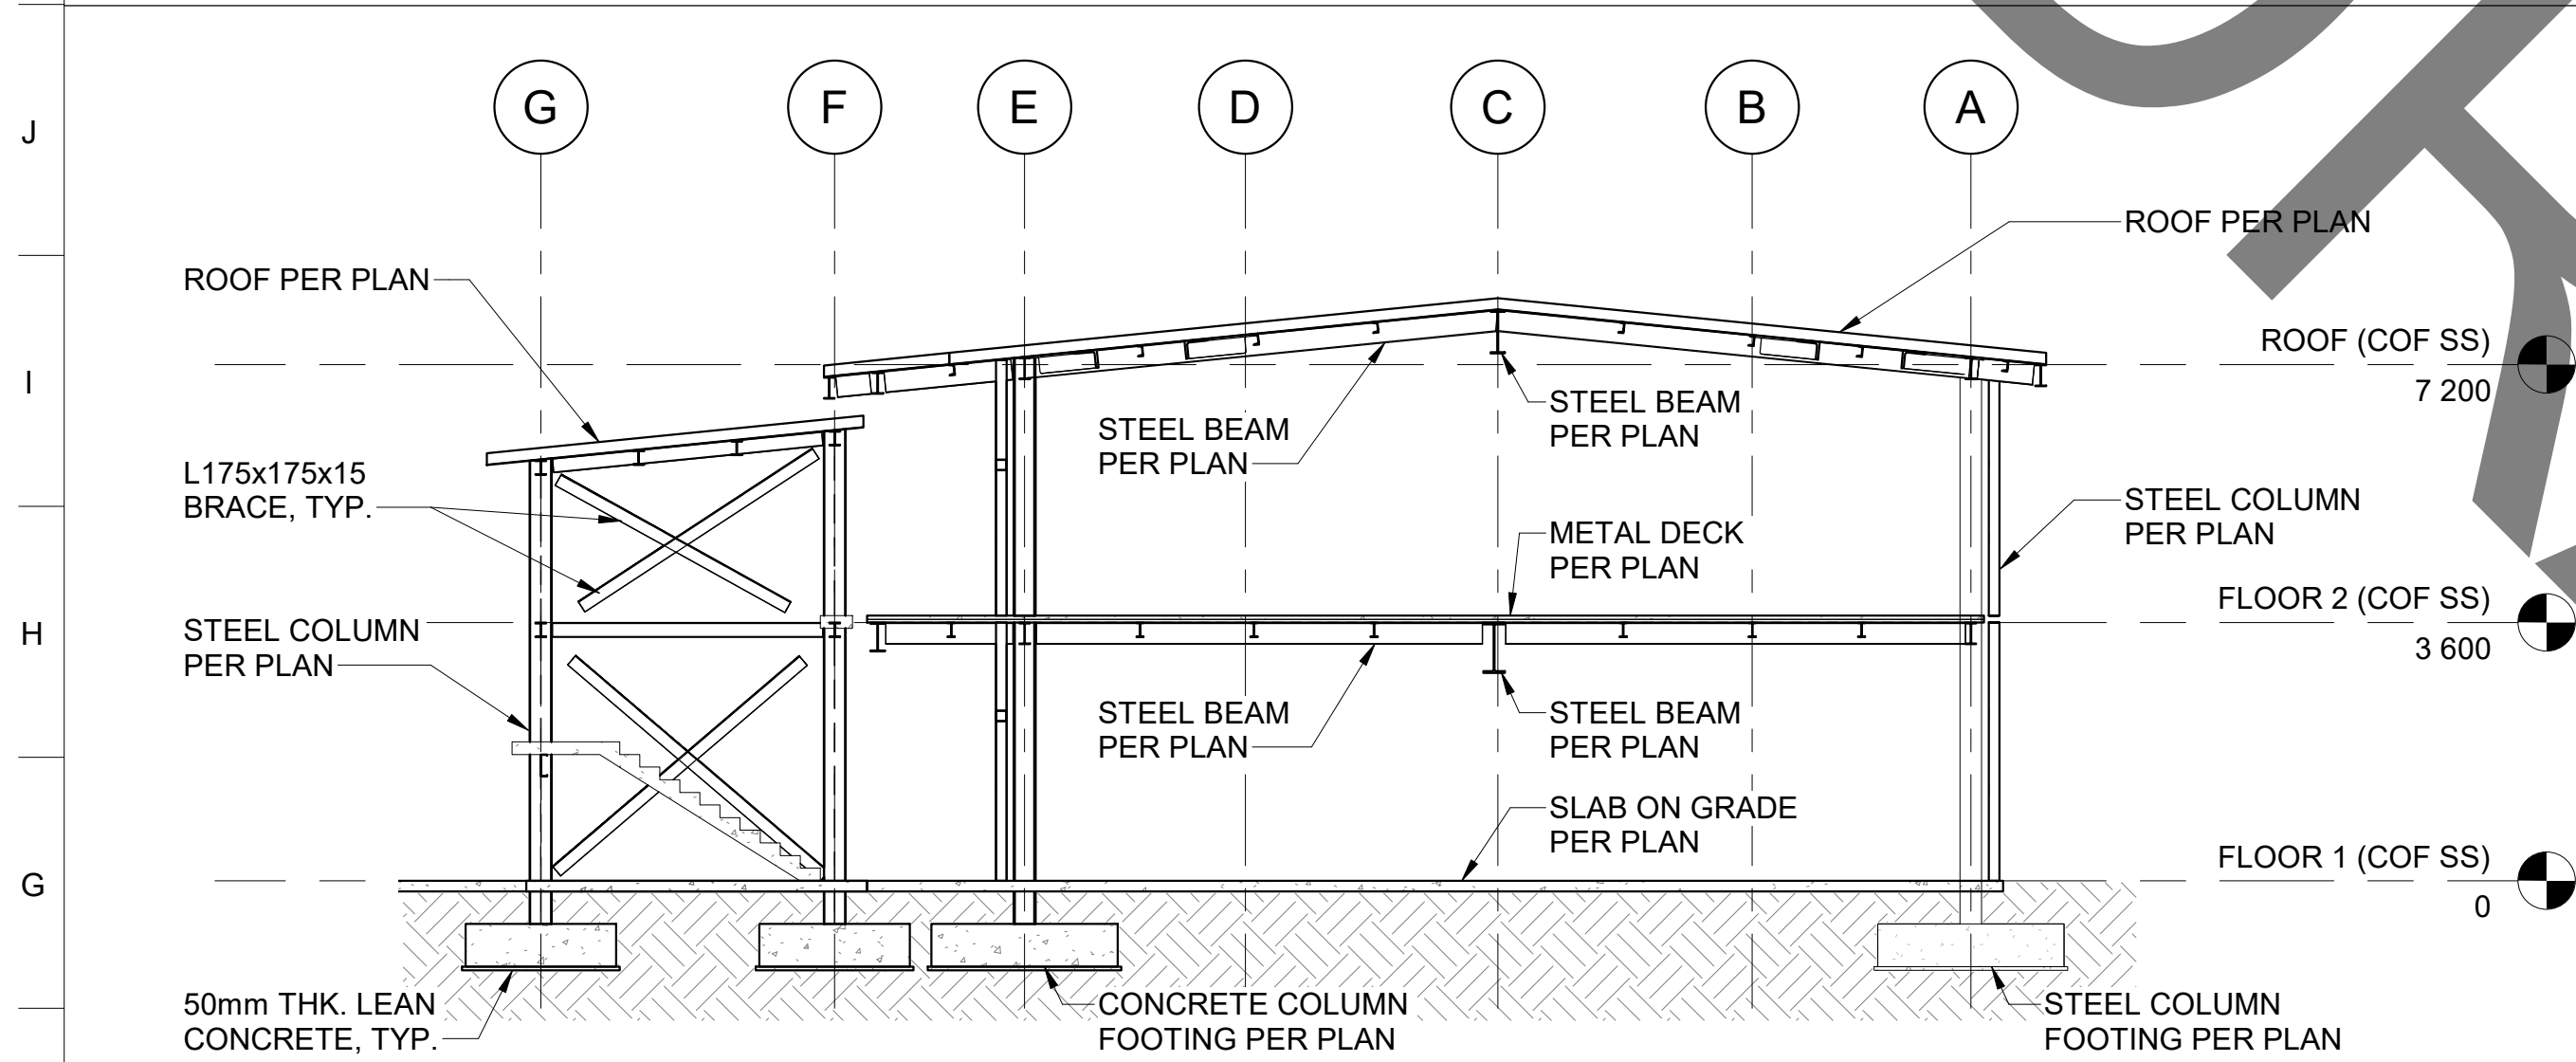

F1 COF SS - BUILDING SECTIONS (CLIN 0004)
SCALE 1 : 100

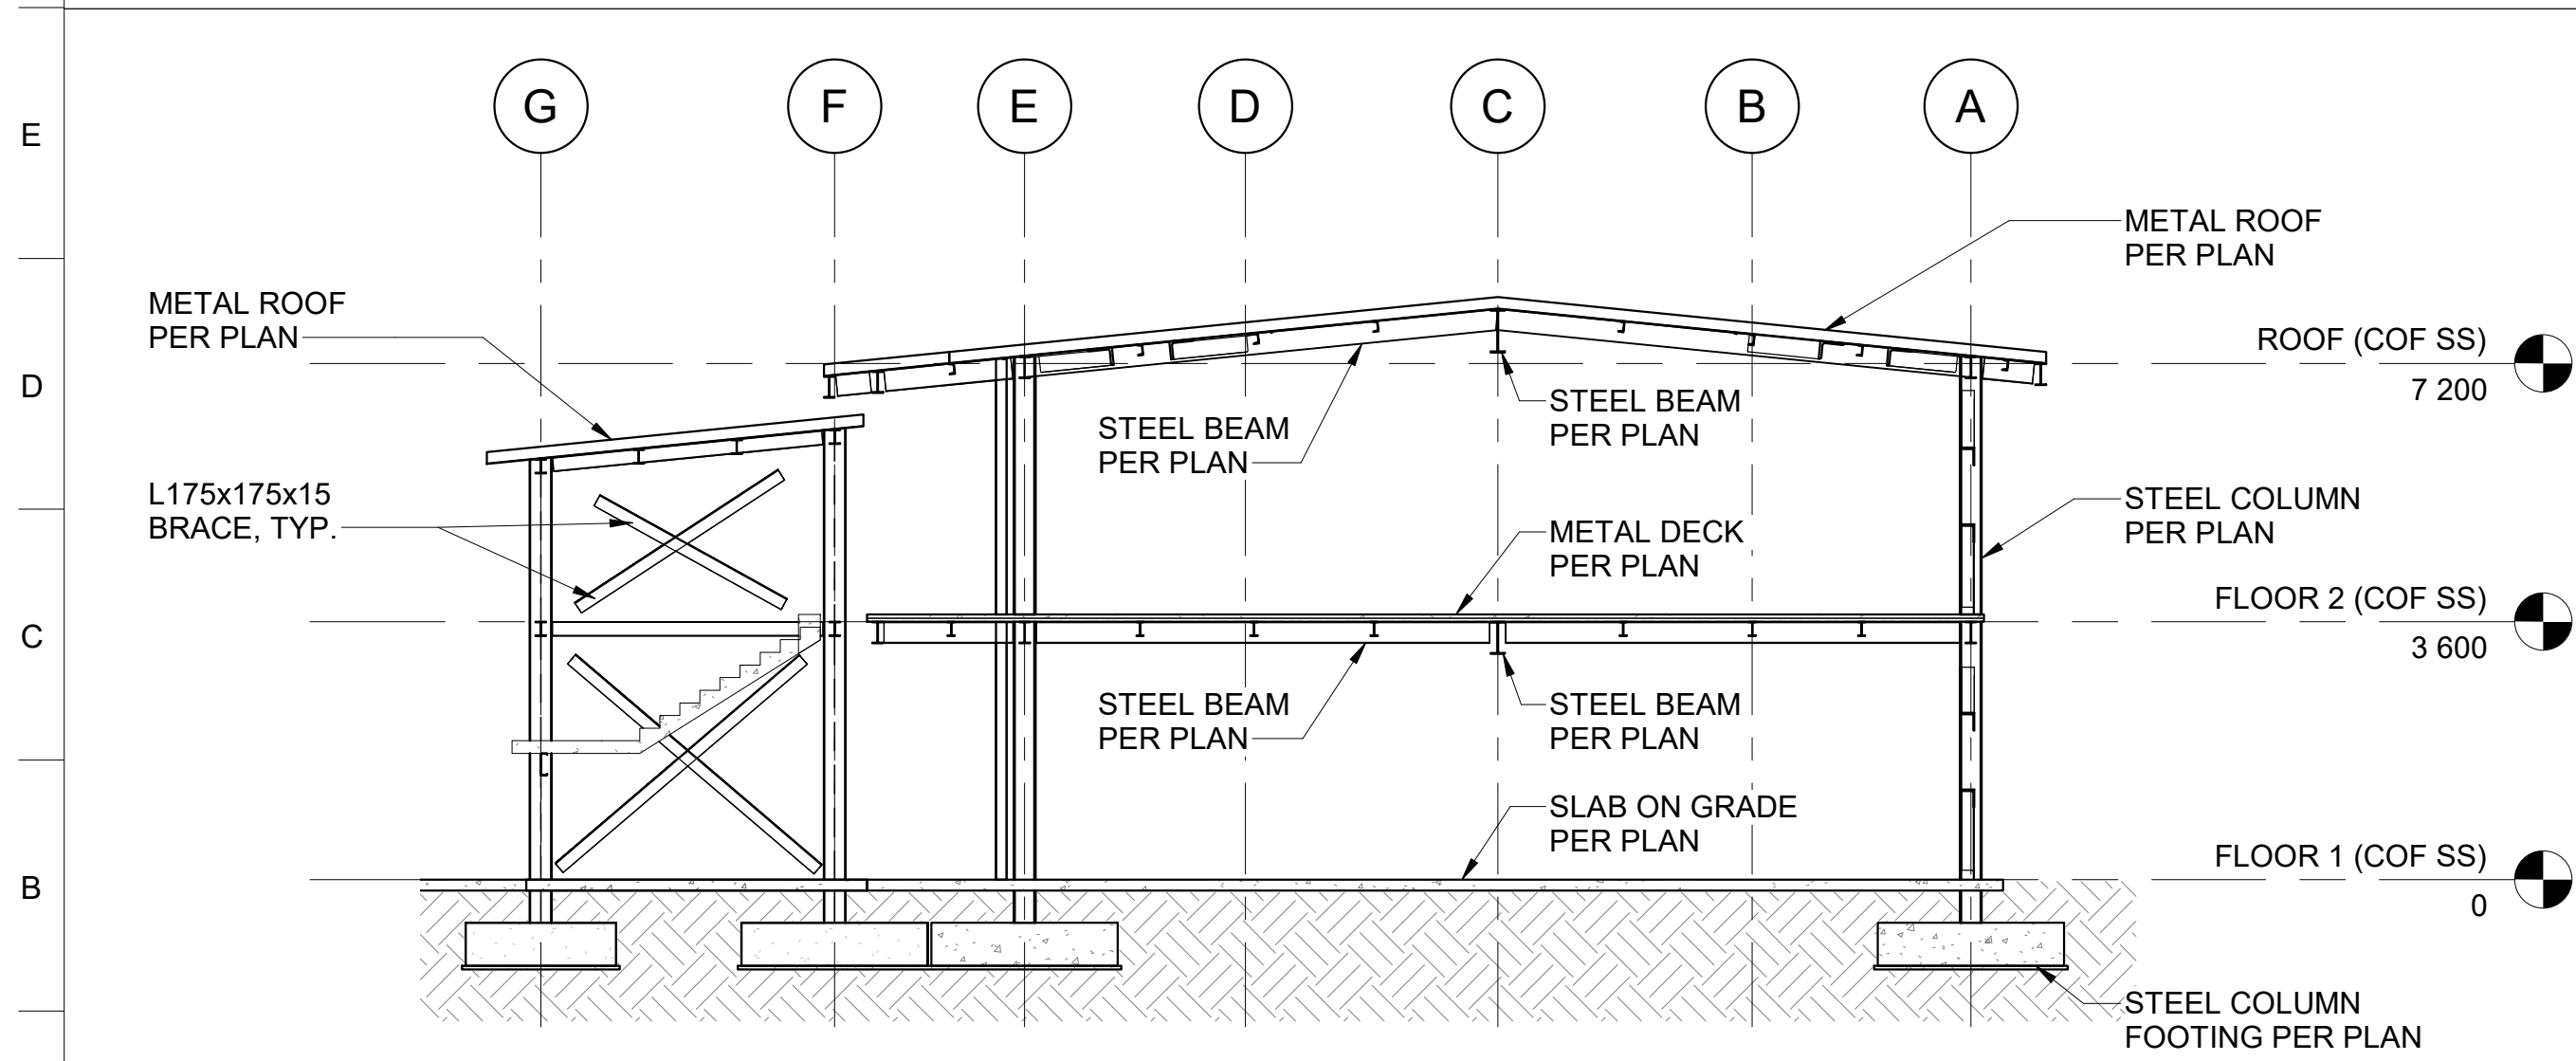

A1 COF SS - BUILDING SECTIONS (CLIN 0004)
SCALE 1 : 100

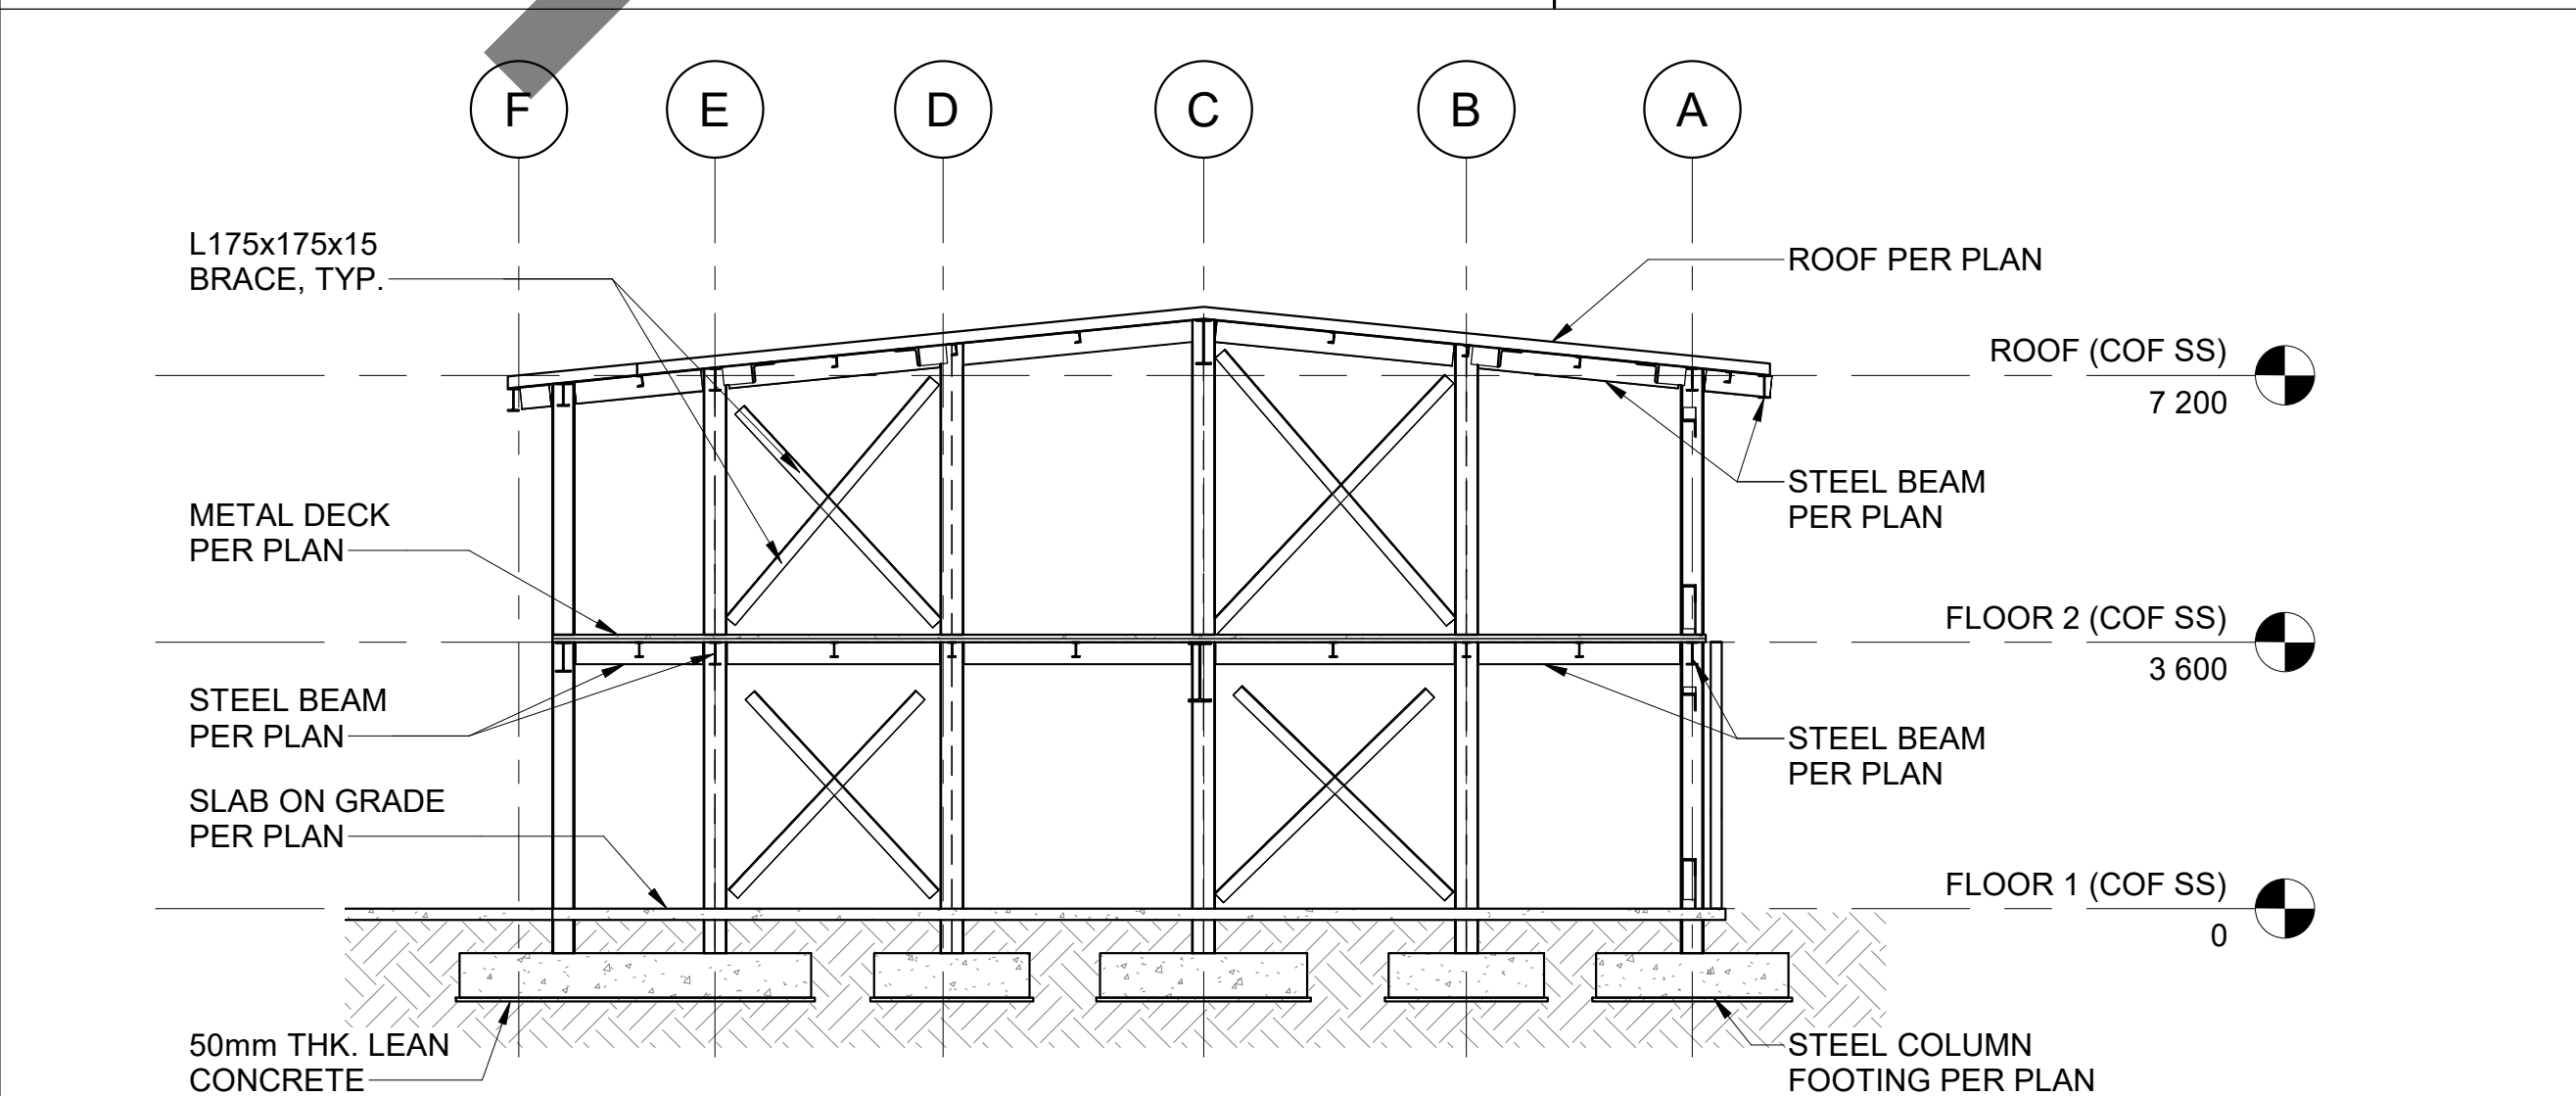

A12 COF SS - BUILDING SECTIONS (CLIN 0004)
SCALE 1 : 100

REFERENCE DRAWINGS

- S-001 - GENERAL NOTES
- S-002 - DESIGN DATA, DESIGN CODES AND STANDARDS, ABBREVIATION
- S-501 - TYPICAL REINFORCING STEEL DETAILS
- S-502 - TYPICAL CONCRETE DETAILS
- S-503 - TYPICAL STEEL DECK DETAILS
- S-504 - TYPICAL STEEL NOTES AND DETAILS
- S-604 - CONCRETE FOOTING SCHEDULE

NOTES


- SEE ARCHITECTURAL DRAWINGS FOR DIMENSIONS, ELEVATIONS AND DETAILS NOT SHOWN ON STRUCTURAL DRAWINGS.
- SEE ARCHITECTURAL DRAWINGS FOR FLOOR SLOPE.
- VERIFY WITH ARCHITECT/MECHANICAL FOR SIZE AND LOCATION OF OPENINGS.

CLIN 0004


GRAPHIC SCALE

GRAPHIC SCALE

SCALE: 1 : 50

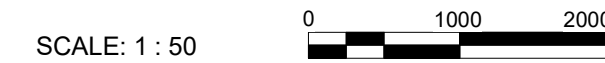

ALL DIMENSIONS AND/OR DIMENSIONS SHOWN IN CALLOUT/NOTES ARE IN MILLIMETERS UNLESS NOTED OTHERWISE.

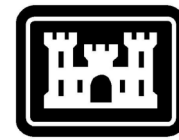

US Army Corps
of Engineers ®

DATE

MARK

DESCRIPTION

ISSUE DATE:

DESIGNED BY:

DRAWN BY:

CHECKED BY:

SUBMITTED BY:

SIZE:

ANSI D

ISSUE DATE:

SOLICITATION NO.:

CONTRACT NO.:

W9124V-17-D-0003

W9124V-17-D-0003

US ARMY CORPS OF ENGINEERS

JAPAN ENGINEER DISTRICT

OKINAWA AREA OFFICE

APO AP 96376-5132

SSFM

SSFM INTERNATIONAL, INC.

501 SUMNER STREET, SUITE 620

HONOLULU, HAWAII 96817

APO AP 96343-5010





FY20 MCA PN7833 VEHICLE MAINTENANCE SHOP

COF SS - BUILDING SECTIONS (CLIN 0004)

SHEET ID

COF

S-H301

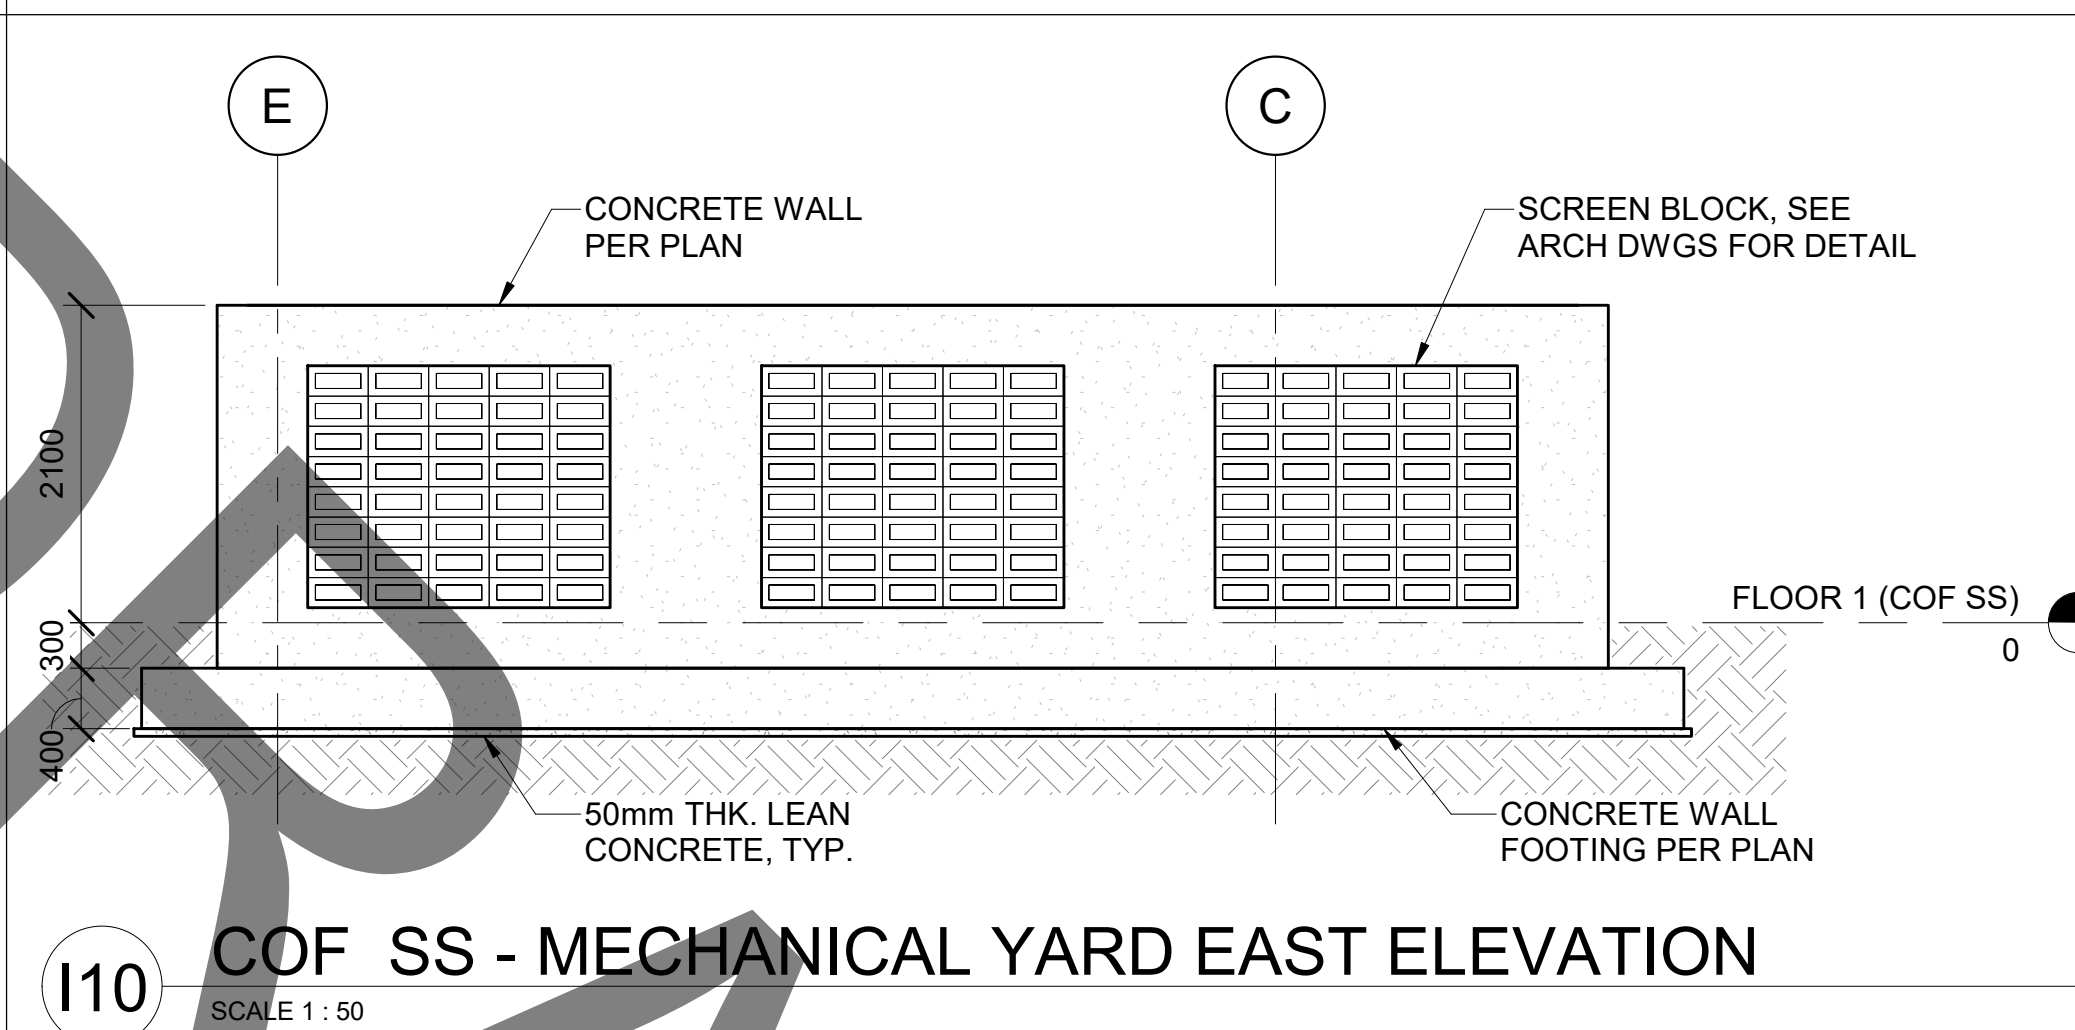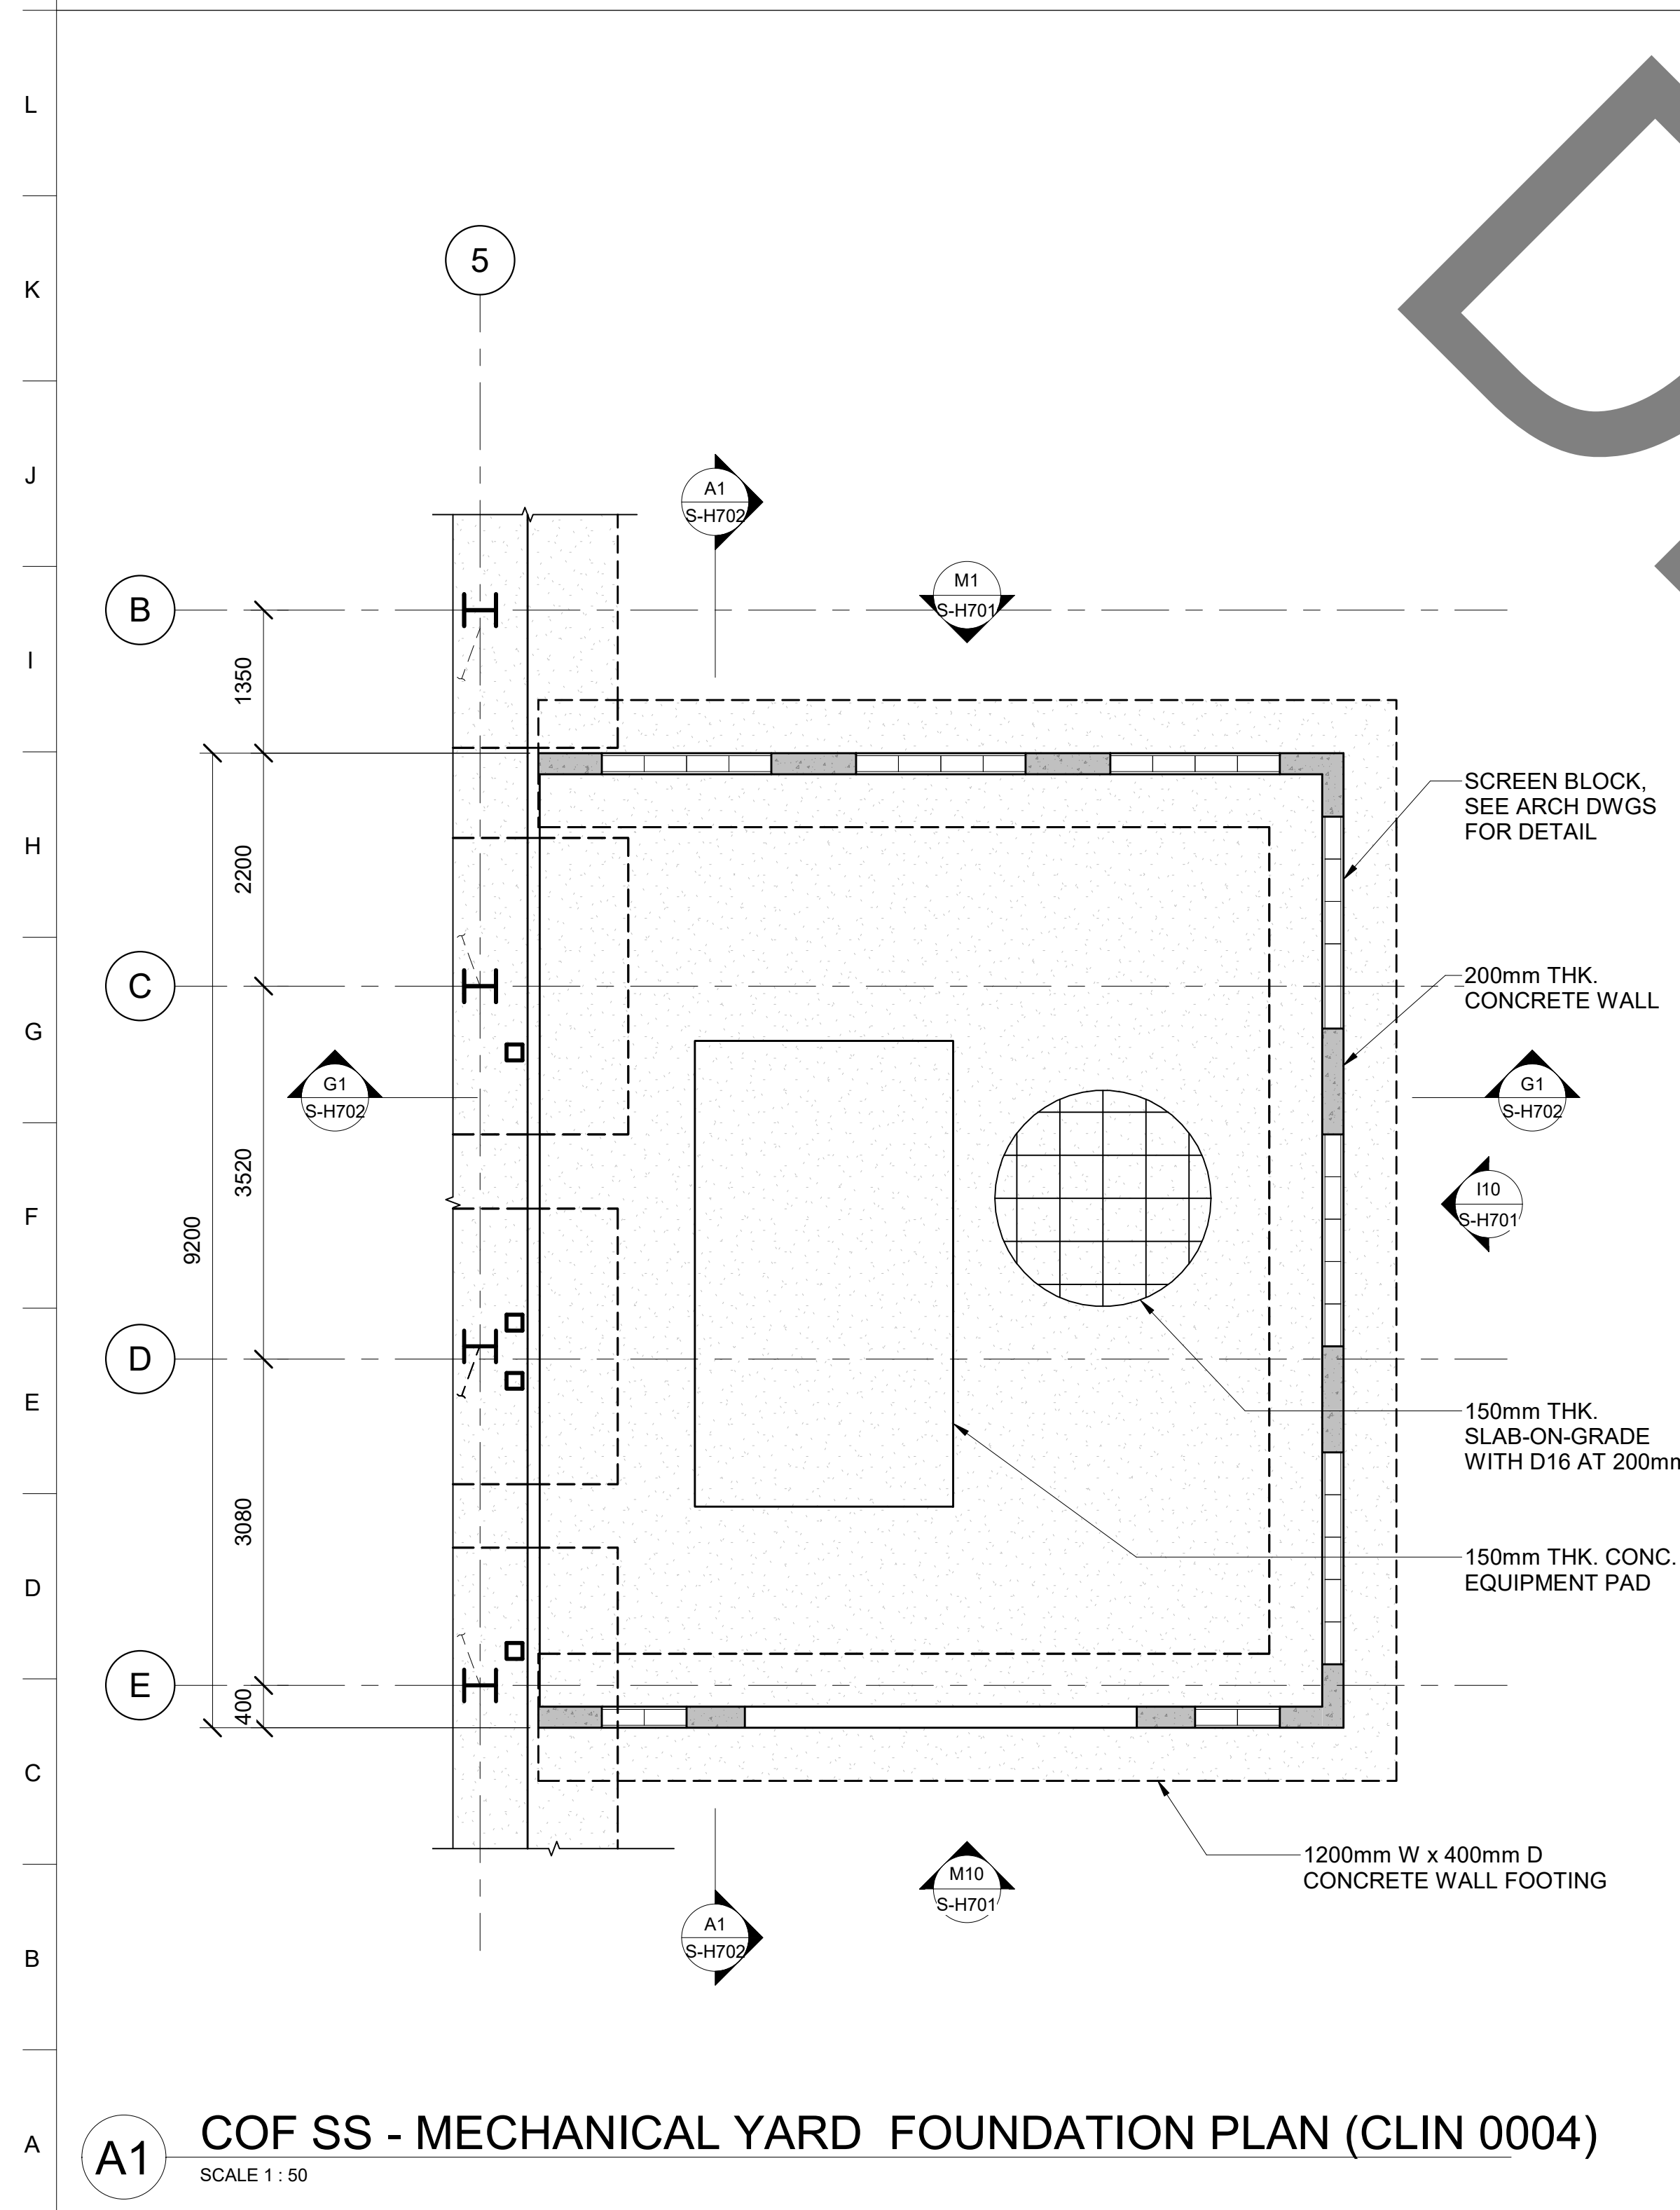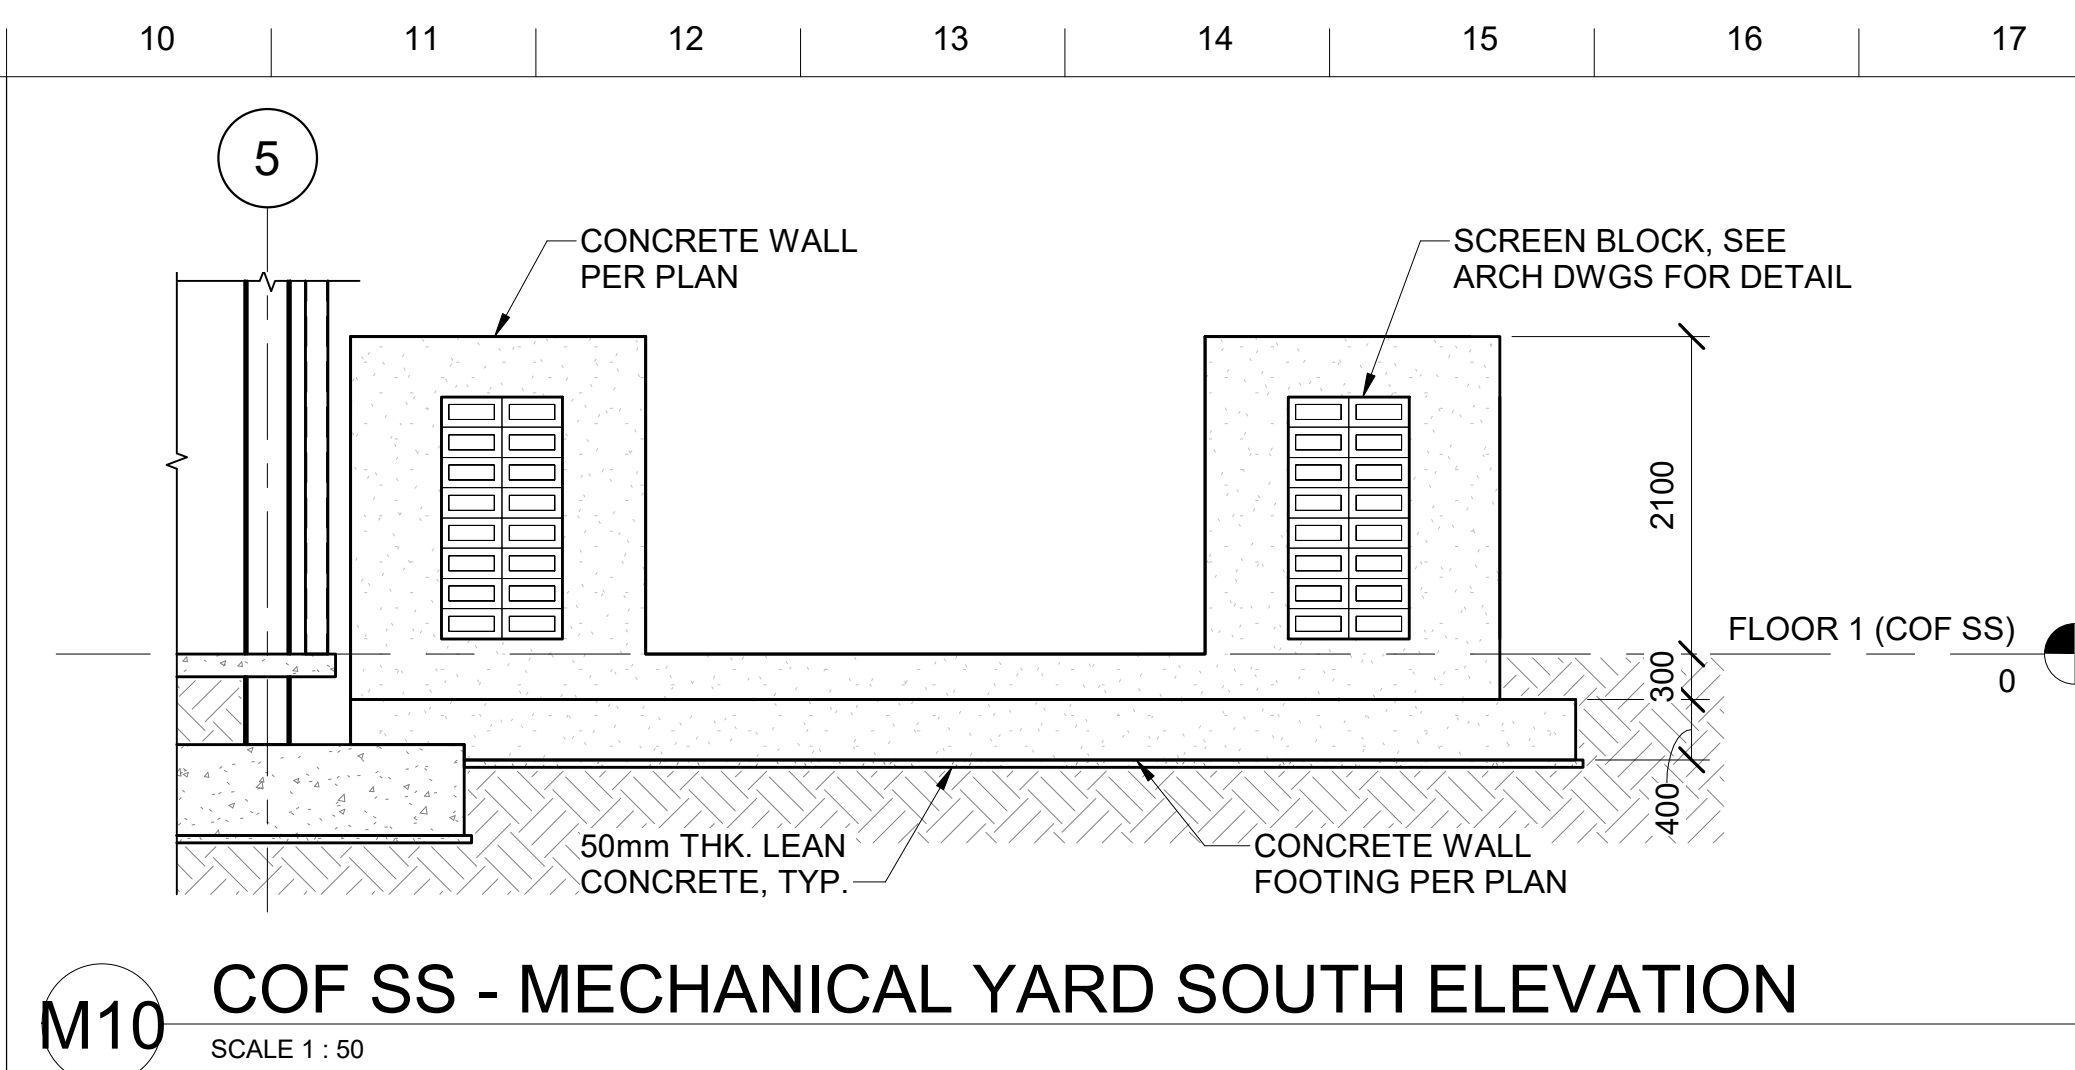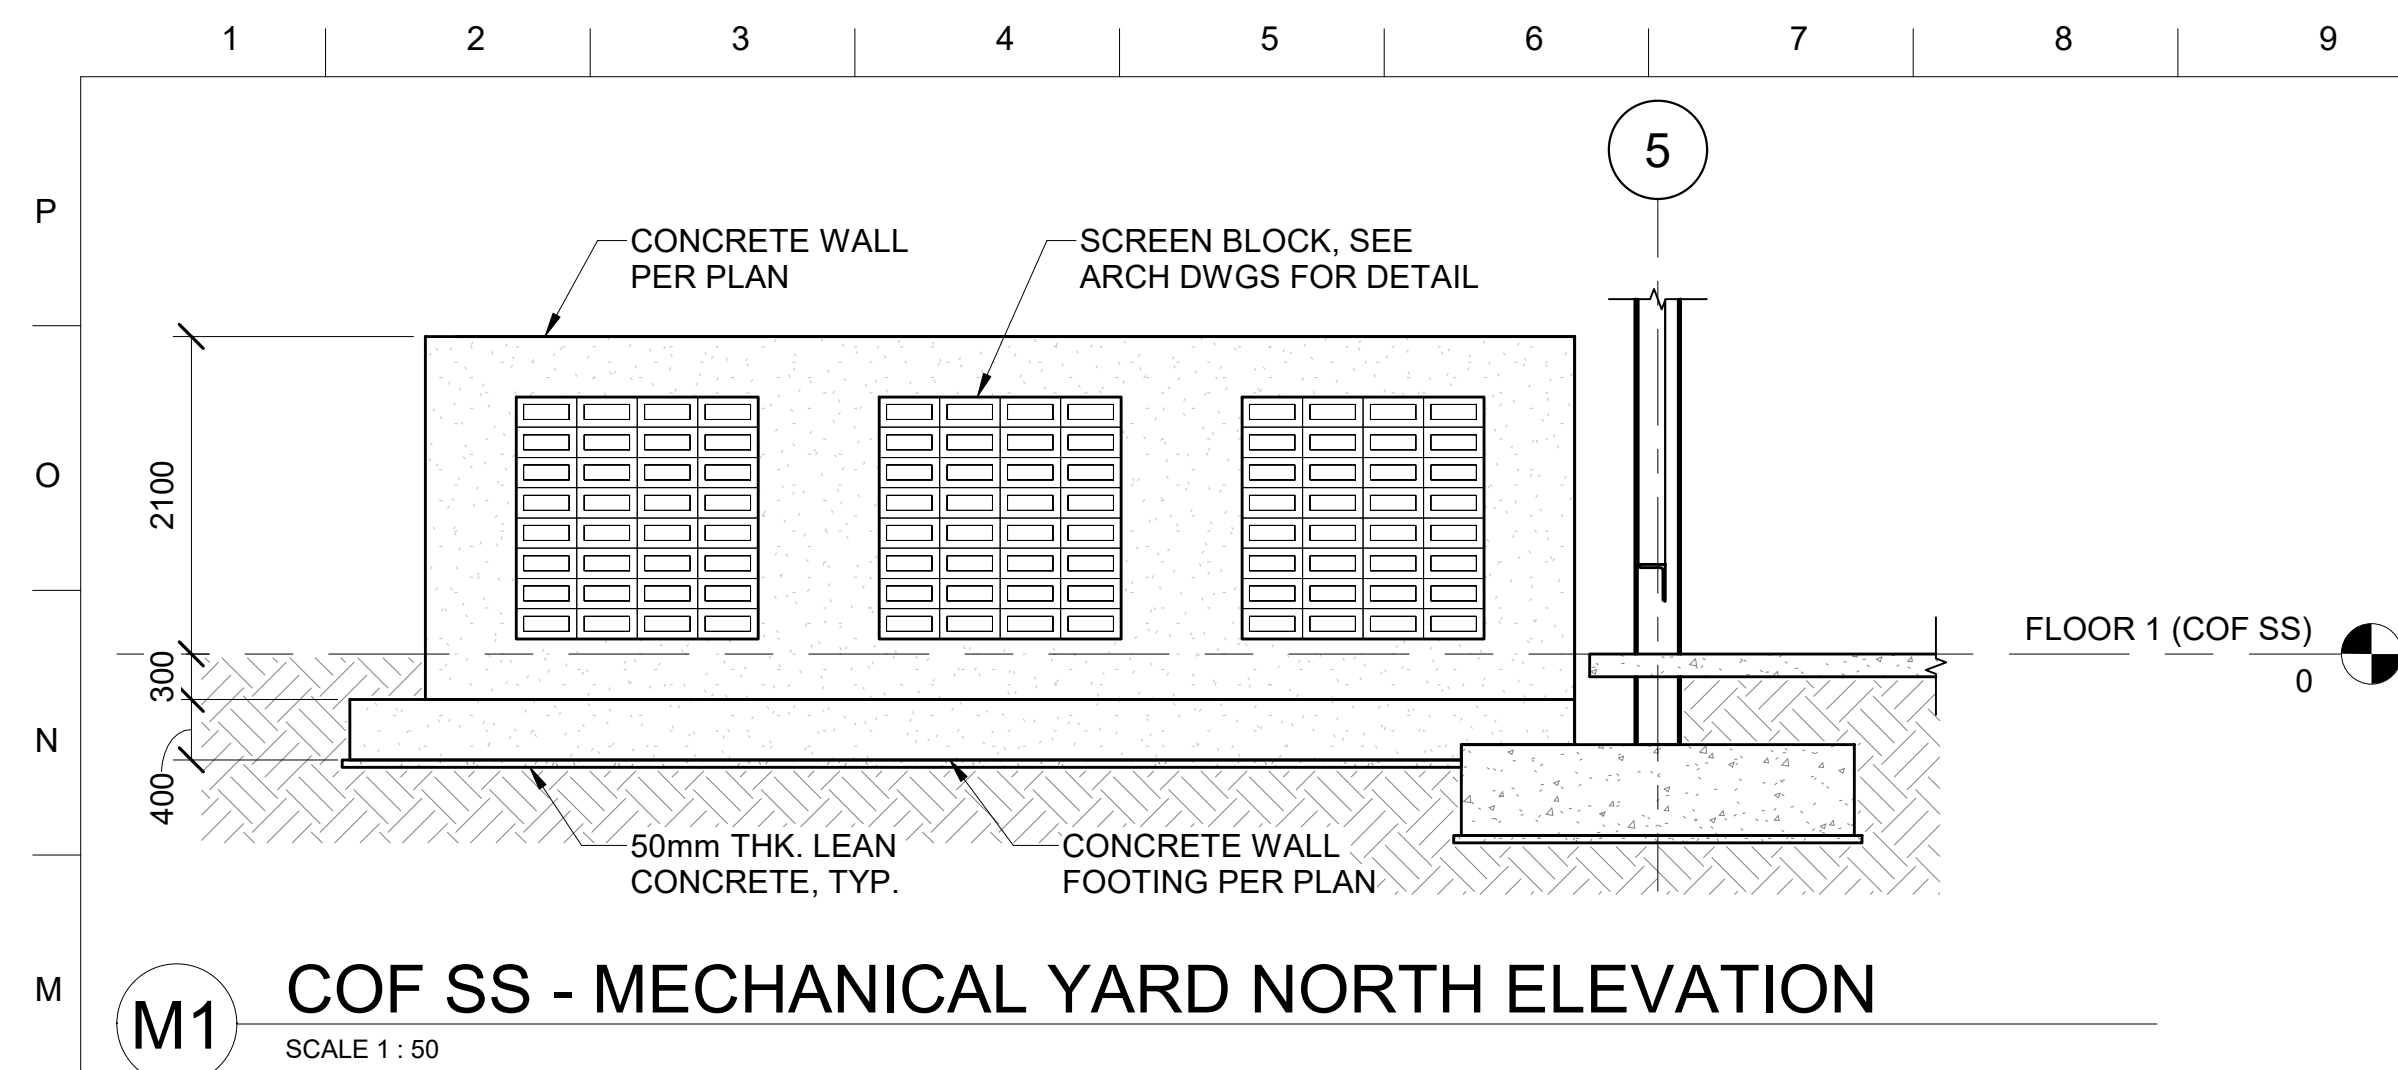

REFERENCE DRAWINGS

S-001 - GENERAL NOTES
S-002 - DESIGN DATA, DESIGN CODES AND STANDARDS,
ABBREVIATION
S-501 - TYPICAL REINFORCING STEEL DETAILS
S-502 - TYPICAL CONCRETE DETAILS
S-604 - CONCRETE FOOTING SCHEDULE
S-605 - CONCRETE WALL SCHEDULE




**S Army Corps
f Engineers ®**

[illegible]

NOTES

1. SEE ARCHITECTURAL DRAWINGS FOR DIMENSIONS, ELEVATIONS AND DETAILS NOT SHOWN ON STRUCTURAL DRAWINGS.
2. SEE ARCHITECTURAL DRAWINGS FOR FLOOR SLOPE.
3. VERIFY WITH ARCHITECT/MECHANICAL FOR SIZE AND LOCATION OF OPENINGS.
4. THICKNESS OF CONCRETE SLABS SHOWN ARE MINIMUM AND MUST BE MAINTAINED AT SLOPED PORTION.
5. SEE CIVIL DRAWINGS FOR FINISH FLOOR ELEVATION.
6. TYP TOP OF SLAB-ONGRADE EL = 0 UNO
7. TYP TOP OF FOOTING EL = -600 UNO

 U.S. ARMY CORPS OF ENGINEERS JANUARY 1987 OKINAWA AREA OFFICE APO AF 96376-5132	 SSFM INTERNATIONAL, INC. 501 KOWALEWICZ DRIVE HONOLULU HAWAII 96817	DRAWN BY C. WASIELEWSKI	SOLICITATION NO.: JUNE 2018
		CHECKED BY: J. UNO	CONTRACT NO.: W912HV-17-D-0003
		SUBMITTED BY: J. UNO	
			APPROVED BY: ANSID

CLIN 0004

GRAPHIC SCALE

GRAPHIC SCALE

SCALE: 1 : 50



ALL DIMENSIONS AND/OR DIMENSIONS SHOWN IN
CALLOUT/ NOTES ARE IN MILLIMETERS UNLESS
NOTED OTHERWISE.

MICA PN77833 VEHICLE MAINTENANCE SHOP

AND ELEVATIONS (CLIN 0004)


SHEET ID
COF
H701

Autodesk Docs://Vehicle Maint Shop Kadena/511758_TEMF_STRUC.M

File Path:

Plot Date: 12/16/2025 3:38:06 PM

INTERMEDIATE DESIGN

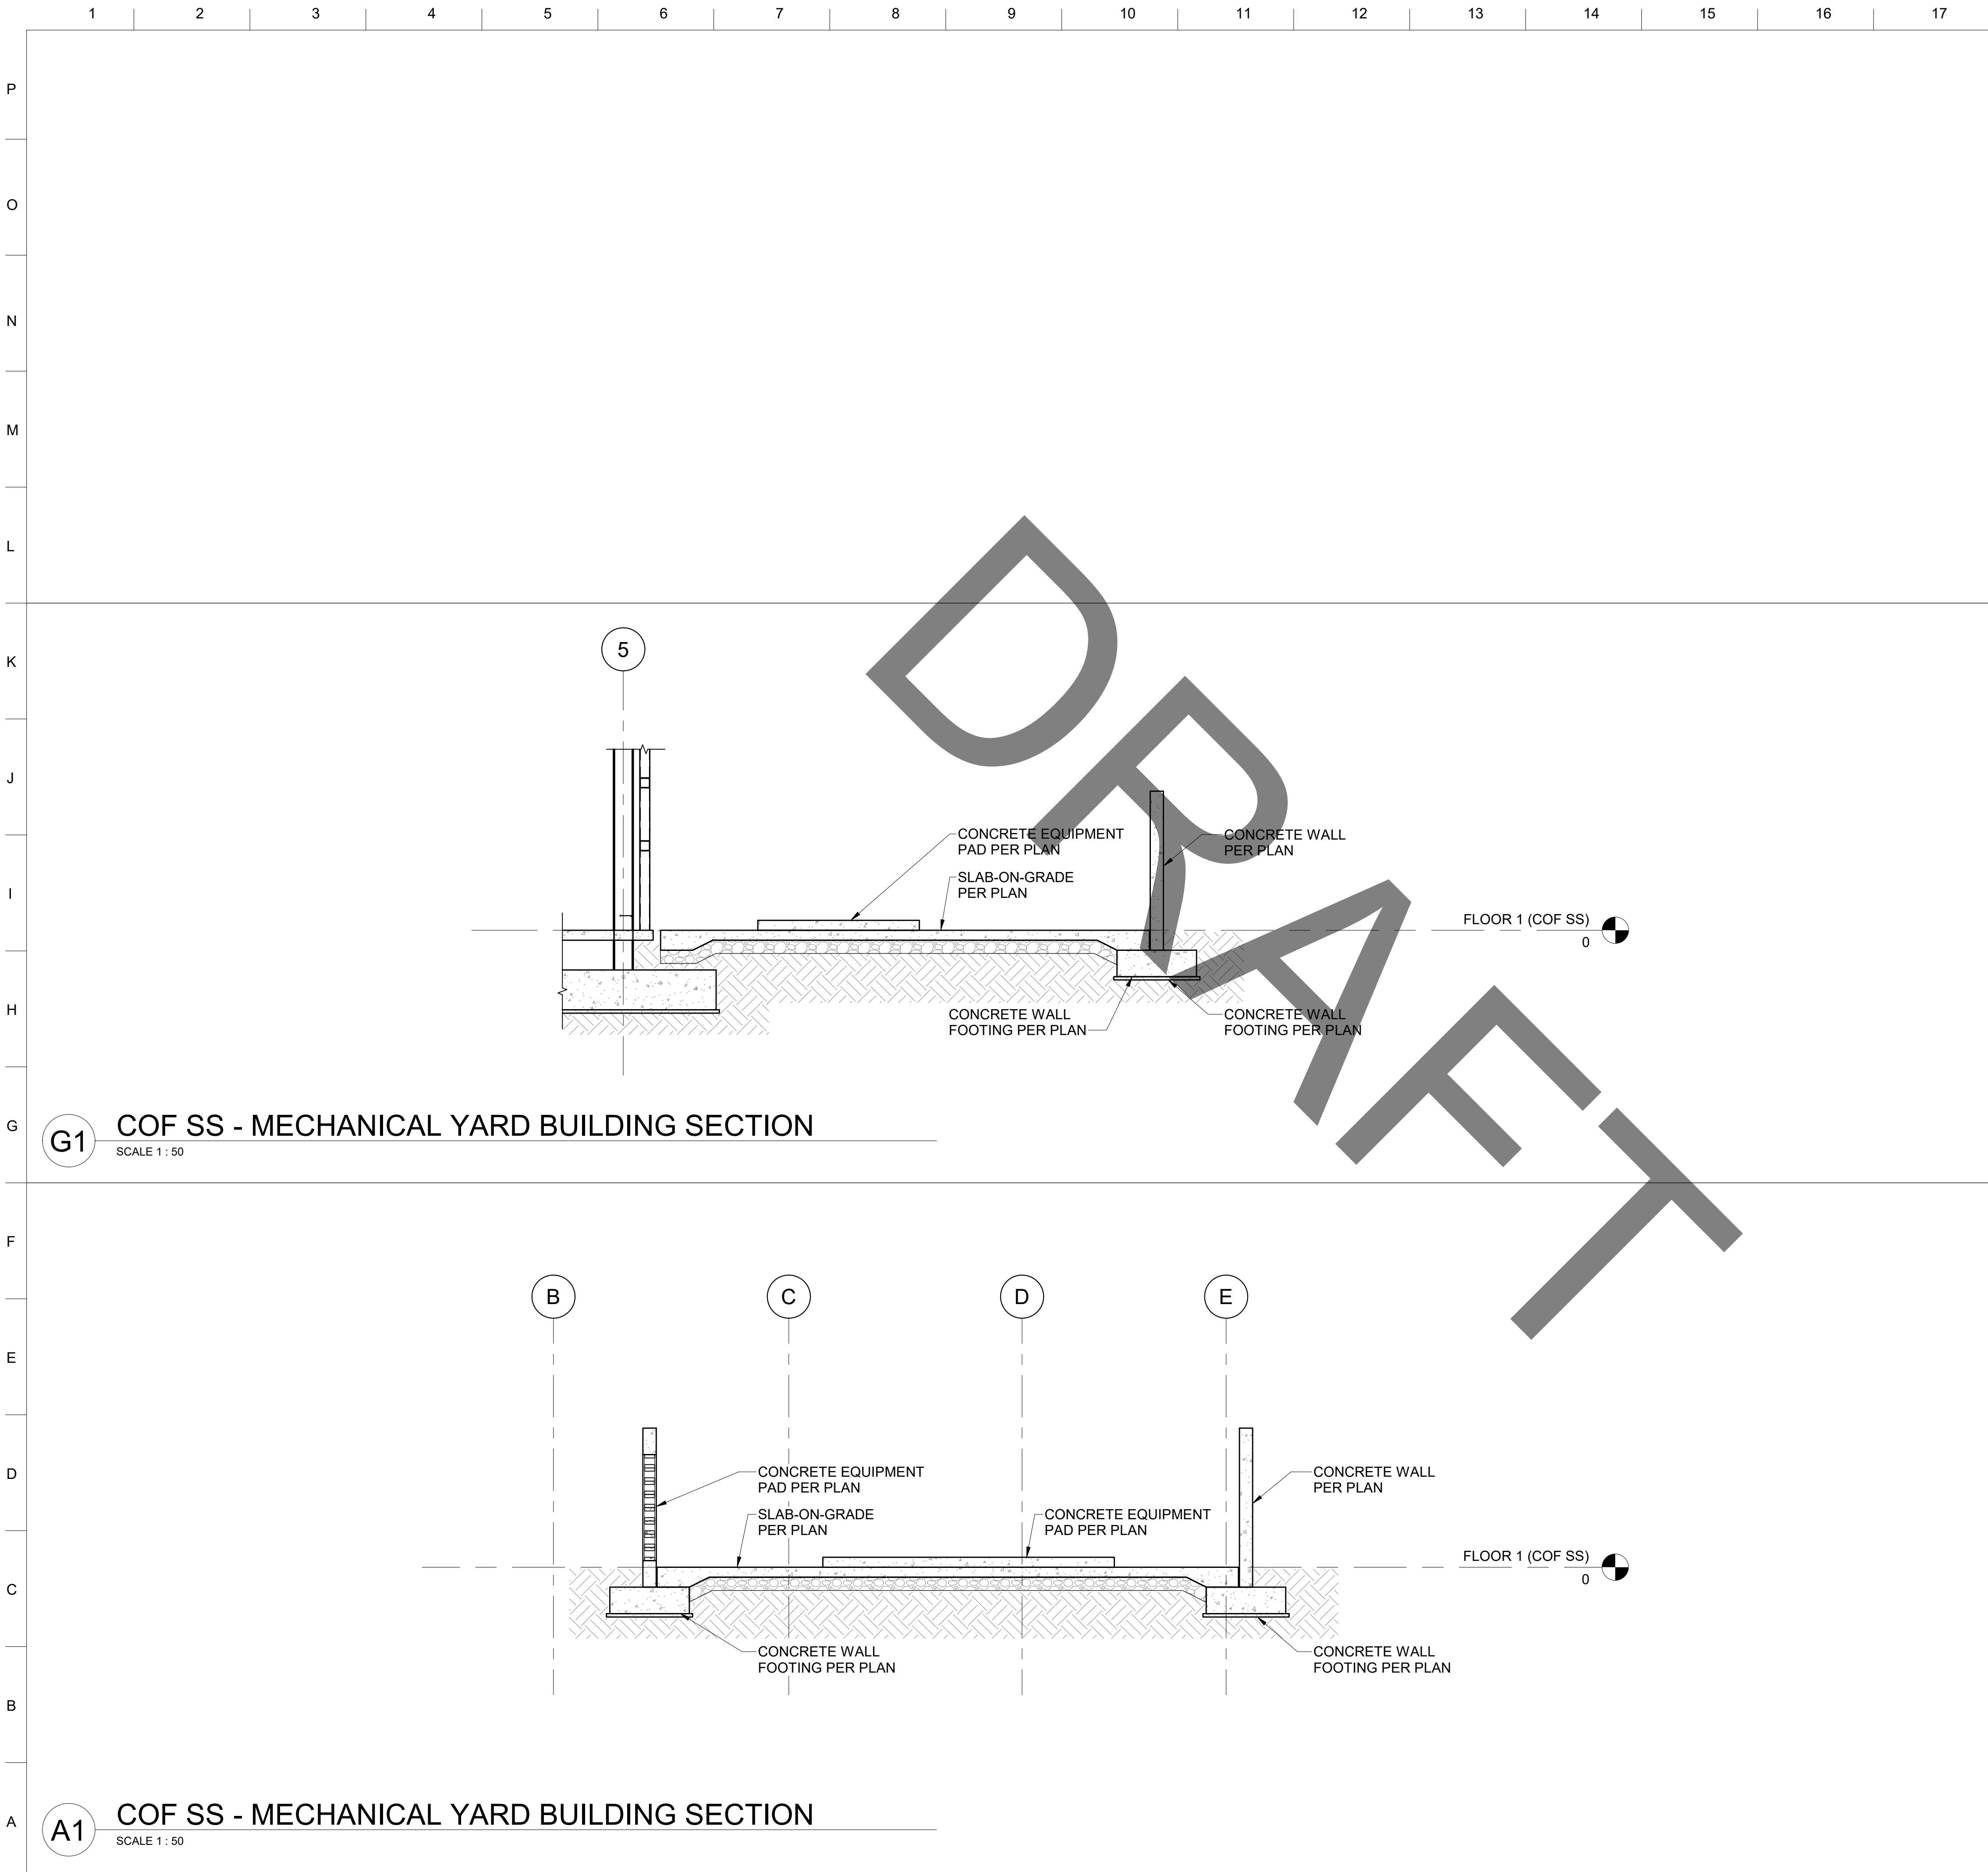

REFERENCE DRAWINGS									
S-001 - GENERAL NOTES S-002 - DESIGN DATA, DESIGN CODES AND STANDARDS, ABBREVIATION S-501 - TYPICAL REINFORCING STEEL DETAILS S-502 - TYPICAL CONCRETE DETAILS S-604 - CONCRETE FOOTING SCHEDULE S-605 - CONCRETE WALL SCHEDULE									

NOTES									
1. SEE ARCHITECTURAL DRAWINGS FOR DIMENSIONS, ELEVATIONS AND DETAILS NOT SHOWN ON STRUCTURAL DRAWINGS. 2. SEE ARCHITECTURAL DRAWINGS FOR FLOOR SLOPE. 3. VERIFY WITH ARCHITECT/MECHANICAL FOR SIZE AND LOCATION OF OPENINGS.									

CLIN 0004									
-----------	--	--	--	--	--	--	--	--	--

GRAPHIC SCALE									
GRAPHIC SCALE SCALE: 1 : 50 ALL DIMENSIONS AND/OR DIMENSIONS SHOWN IN CALLOUT/ NOTES ARE IN MILLIMETERS UNLESS NOTED OTHERWISE.									

US Army Corps of Engineers ®

MARK	DESCRIPTION	DATE

DESIGNED BY: C. WASIELEWSKI	ISSUE DATE: JUNE 2018
DRAWN BY: R. TANGONAN	SOLICITATION NO.:
CHECKED BY: 	CONTRACT NO.: W72BY-17-D-0003
SUBMITTED BY: J. UNO	
SIZE: ANSI D	


US ARMY CORPS OF ENGINEERS
JAPAN ENGINEER DISTRICT
OKINAWA AREA OFFICE
APO AP 96376-5132

SSFM
STRUCTURAL STEEL FABRICATING & MATERIALS, INC.
507 SUMNER STREET, SUITE 620
HONOLULU, HAWAII 96817

APO AP 96343-5010
FY20 MCA PN77833 VEHICLE MAINTENANCE SHOP

COF SS - MECHANICAL YARD BUILDING
SECTIONS (CLIN 0004)

SHEET ID
COF
S-H702

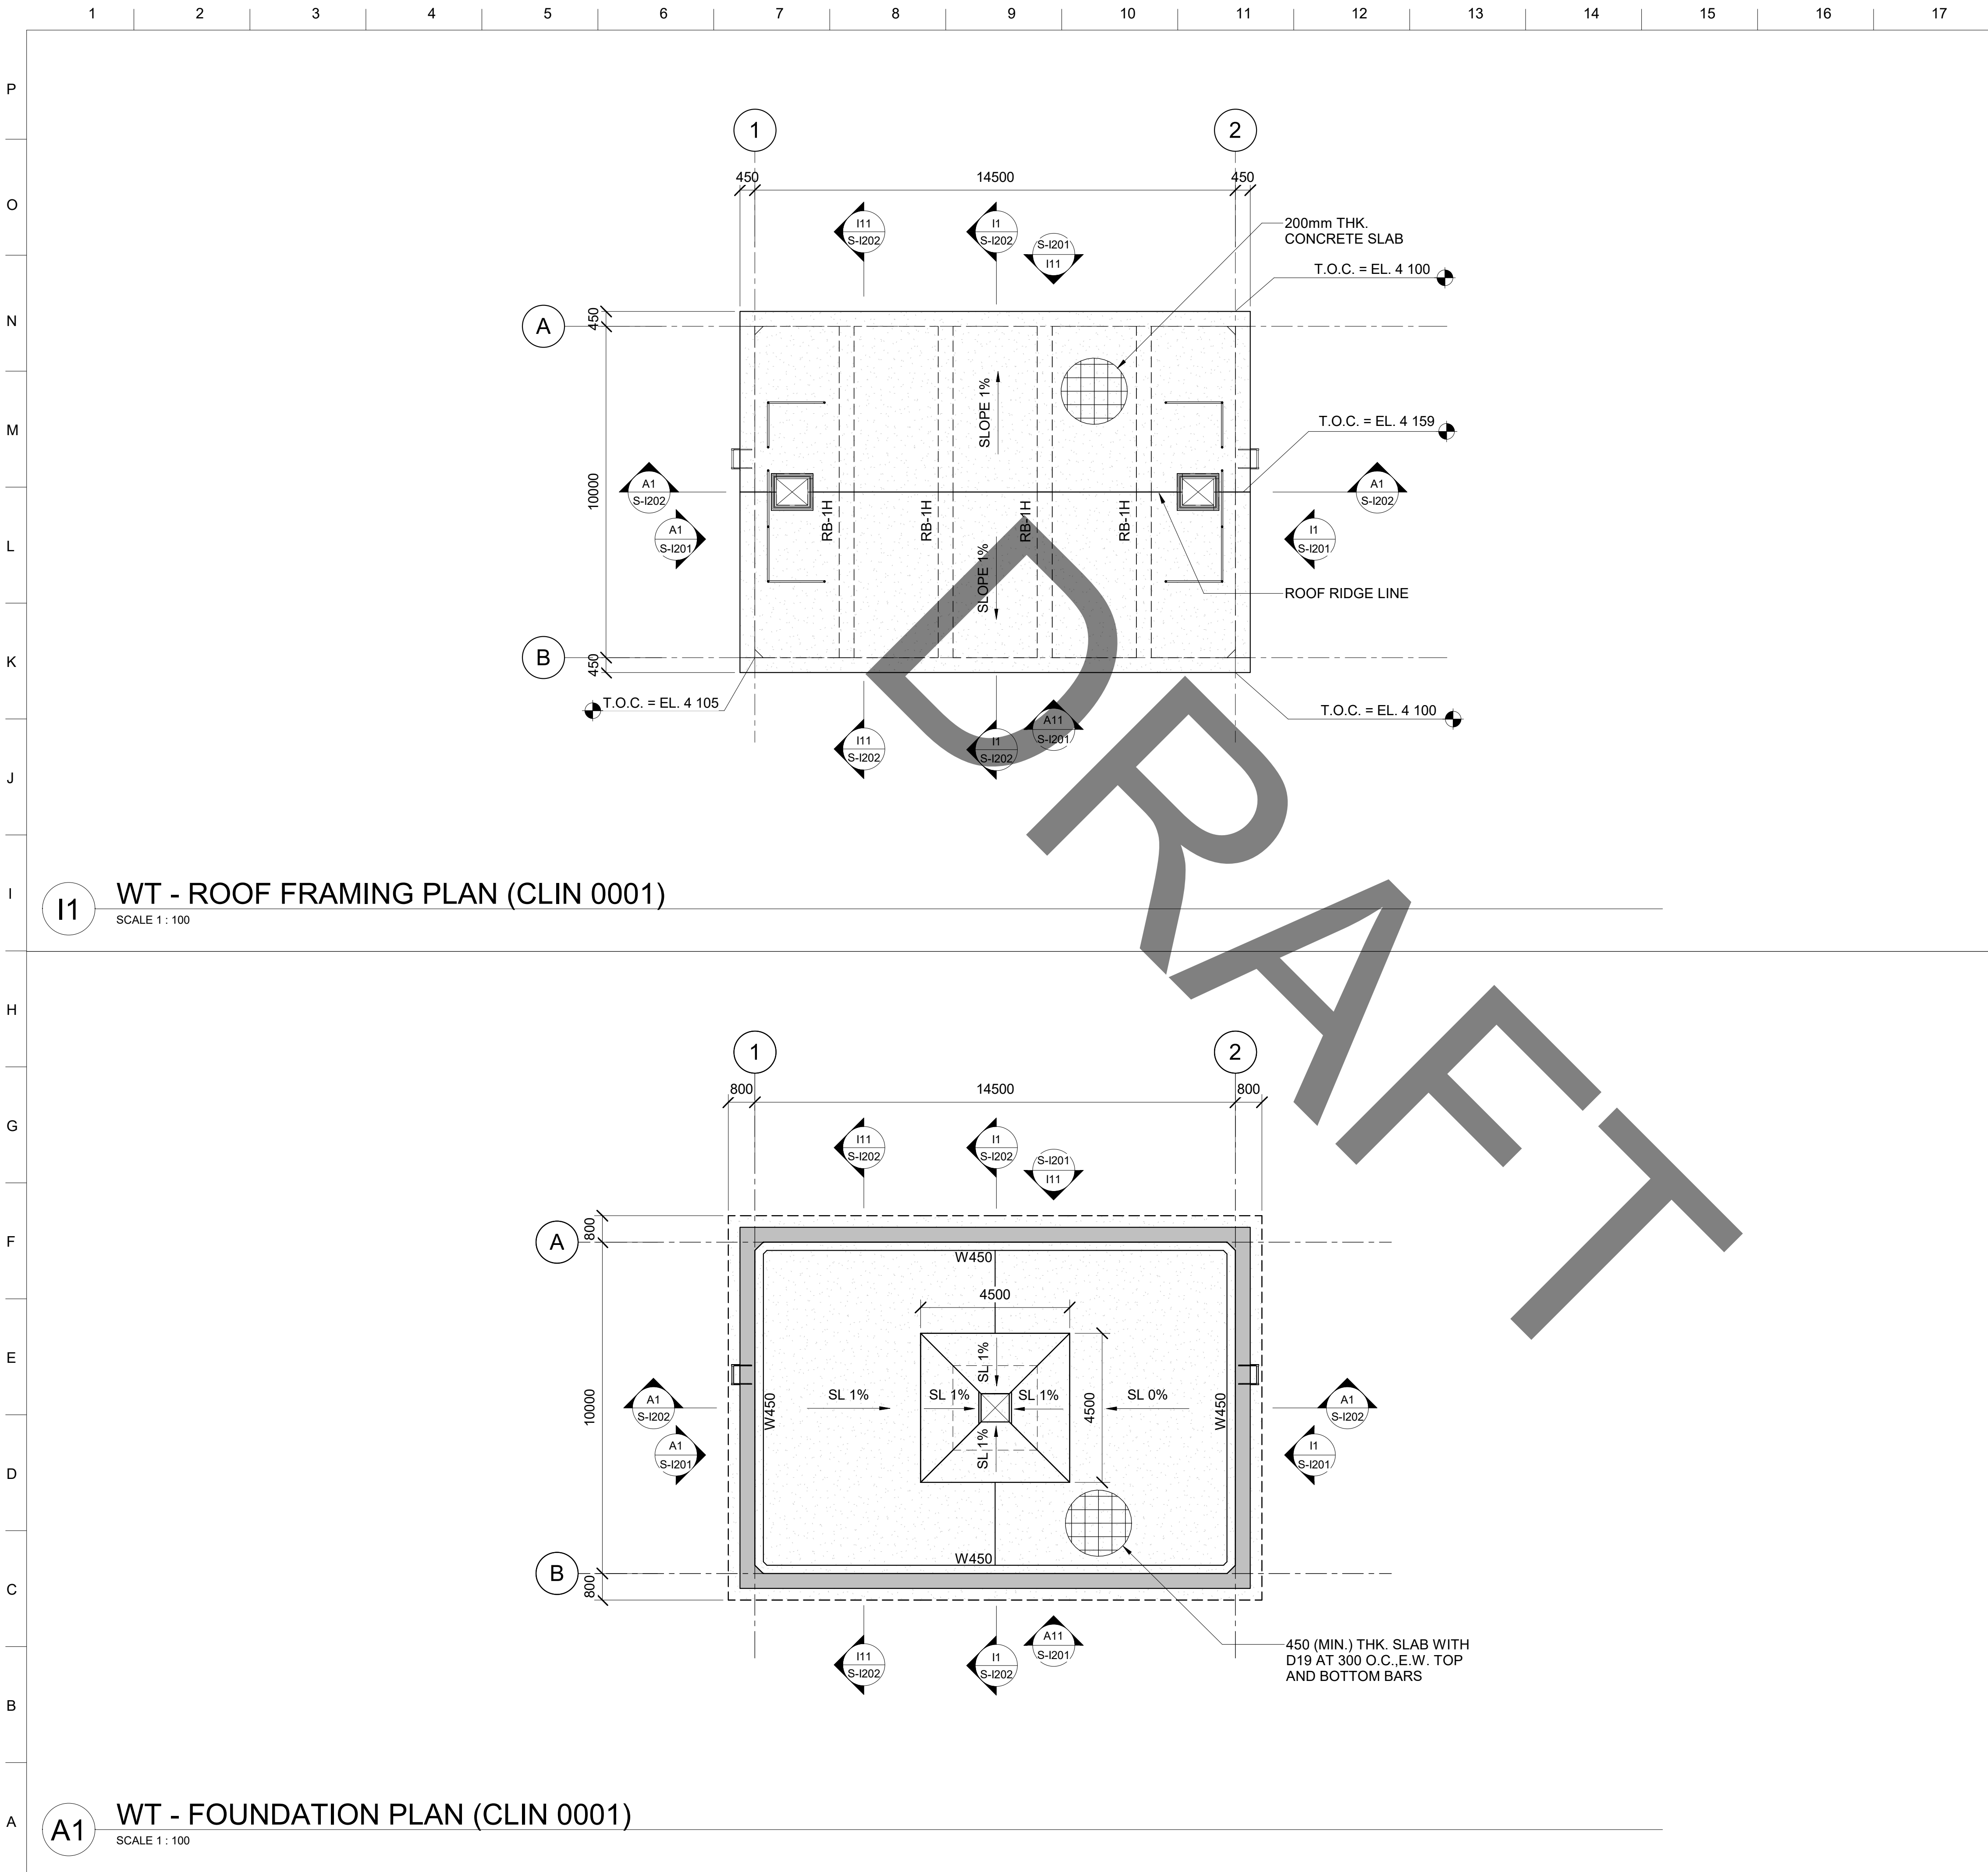

REFERENCE DRAWINGS

S-001 - GENERAL NOTES
S-002 - DESIGN DATA, DESIGN CODES AND STANDARDS, ABBREVIATION
S-501 - TYPICAL REINFORCING STEEL DETAILS
S-605 - CONCRETE WALL SCHEDULE
S-608 - CONCRETE BEAM DETAIL
S-609 - CONCRETE BEAM SCHEDULE

LEGEND

W-X DENOTES CONCRETE WALL
F-X DENOTES CONCRETE COLUMN FOOTING

NOTES

- SEE ARCHITECTURAL DRAWINGS FOR DIMENSIONS, ELEVATIONS AND DETAILS NOT SHOWN ON STRUCTURAL DRAWINGS.
- SEE ARCHITECTURAL DRAWINGS FOR FLOOR SLOPE.
- VERIFY WITH ARCHITECT/MECHANICAL FOR SIZE AND LOCATION OF OPENINGS.
- THICKNESS OF CONCRETE SLABS SHOWN ARE MINIMUM AND MUST BE MAINTAINED AT SLOPED PORTION.
- SEE CIVIL DRAWINGS FOR FINISH FLOOR ELEVATION.
- TYPICAL TOP OF SLAB-ON-GRADE EL = 0 UNO

CLIN 0001

PLAN NORTH

GRAPHIC SCALE

SCALE: 1 : 100

ALL DIMENSIONS AND/OR DIMENSIONS SHOWN IN CALLOUT/ NOTES ARE IN MILLIMETERS UNLESS NOTED OTHERWISE.

US Army Corps of Engineers®

ISSUE DATE:
JUNE 2018

SOLICITATION NO.:
CONTRACT NO.:
W912AV-17-D-0003

DESIGNED BY:
J. RABANAL

DRAWN BY:
R. TANGONAN

CHECKED BY:
J. UNO

SUBMITTED BY:
J. UNO

SIZE:
ANSI D

US ARMY CORPS OF ENGINEERS
JAPAN ENGINEER DISTRICT
OKINAWA AREA OFFICE
APO AP 96376-5132

SSFM
STRUCTURAL STEEL FABRICATION, INC.
501 SUMNER STREET, SUITE 620
HONOLULU, HAWAII 96817

APO AP 96343-5010
FY20 MCA PN77833 VEHICLE MAINTENANCE SHOP


WATER TANK- FOUNDATION AND FRAMING PLAN
(CLIN 0001)

SHEET ID
WT
S-I101


INTERMEDIATE DESIGN

Plot Date: 12/16/2025 3:38:08 PM


File Path: AutoCAD Docs/Vehicle Maint Shop/Kadena511736_TEMF_STRUCT.rvt

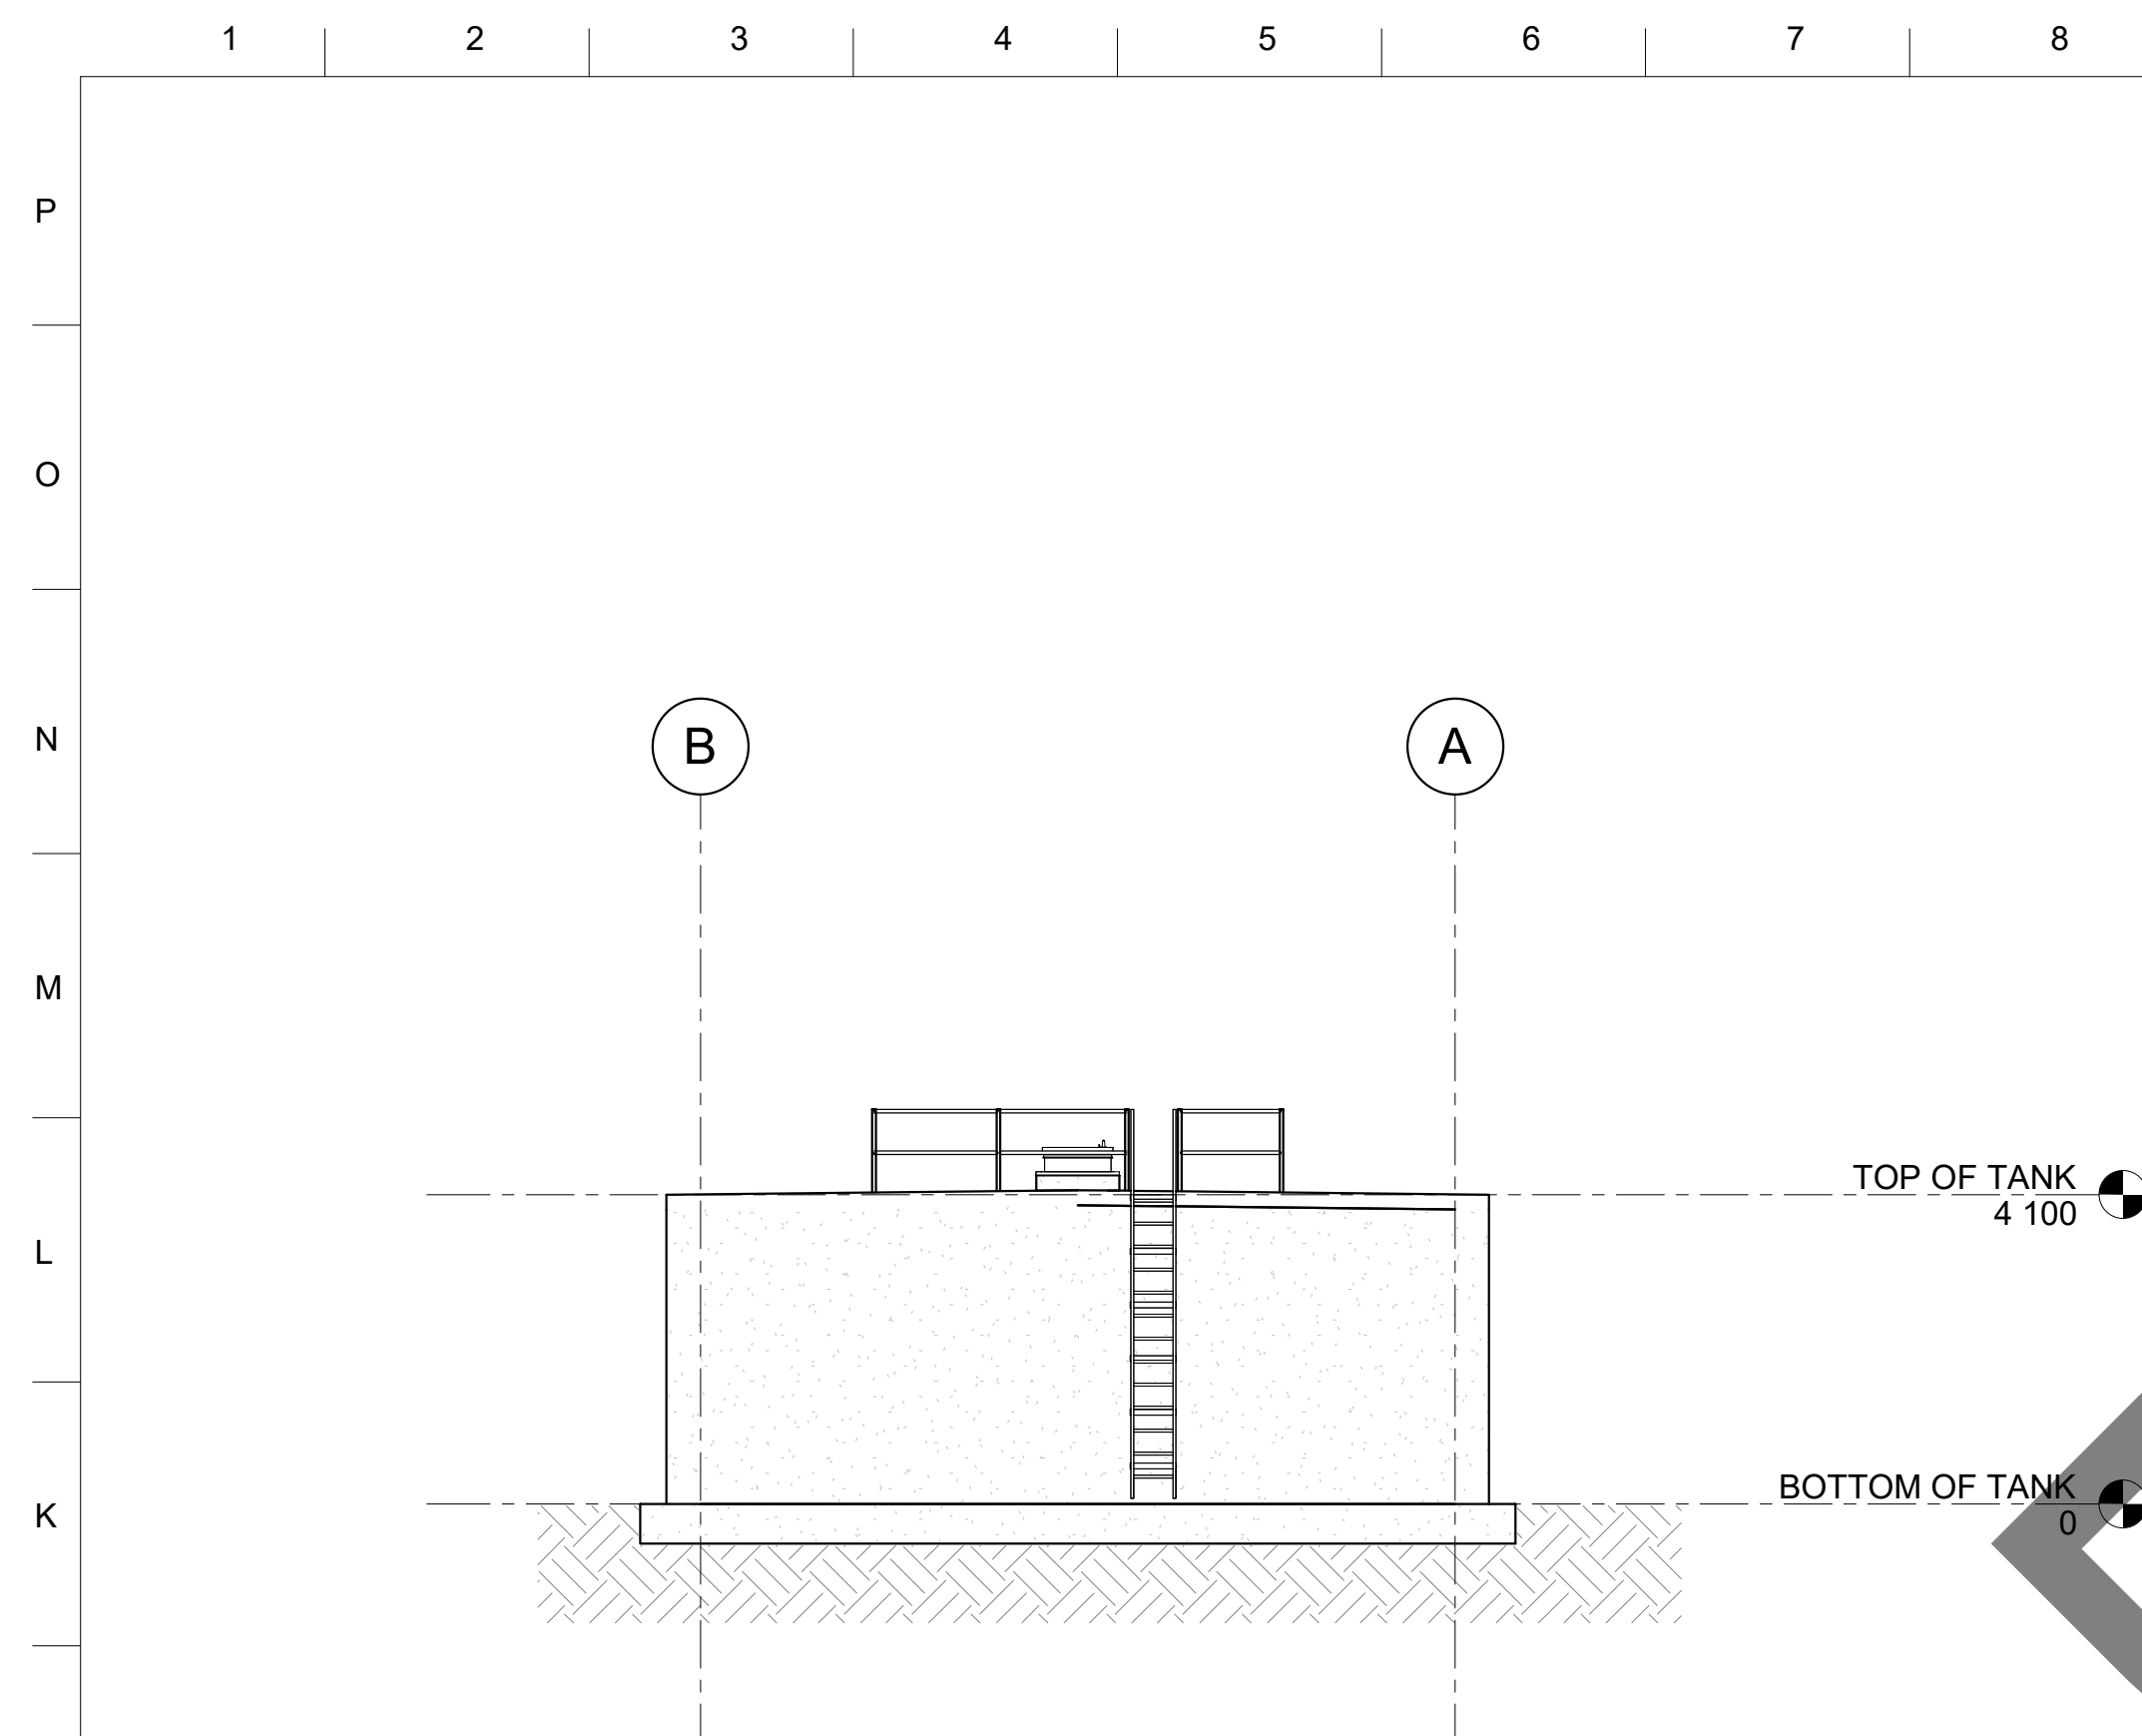


11 WT - EXTERIOR ELEVATION EAST (CLIN 0001)
SCALE 1 : 100

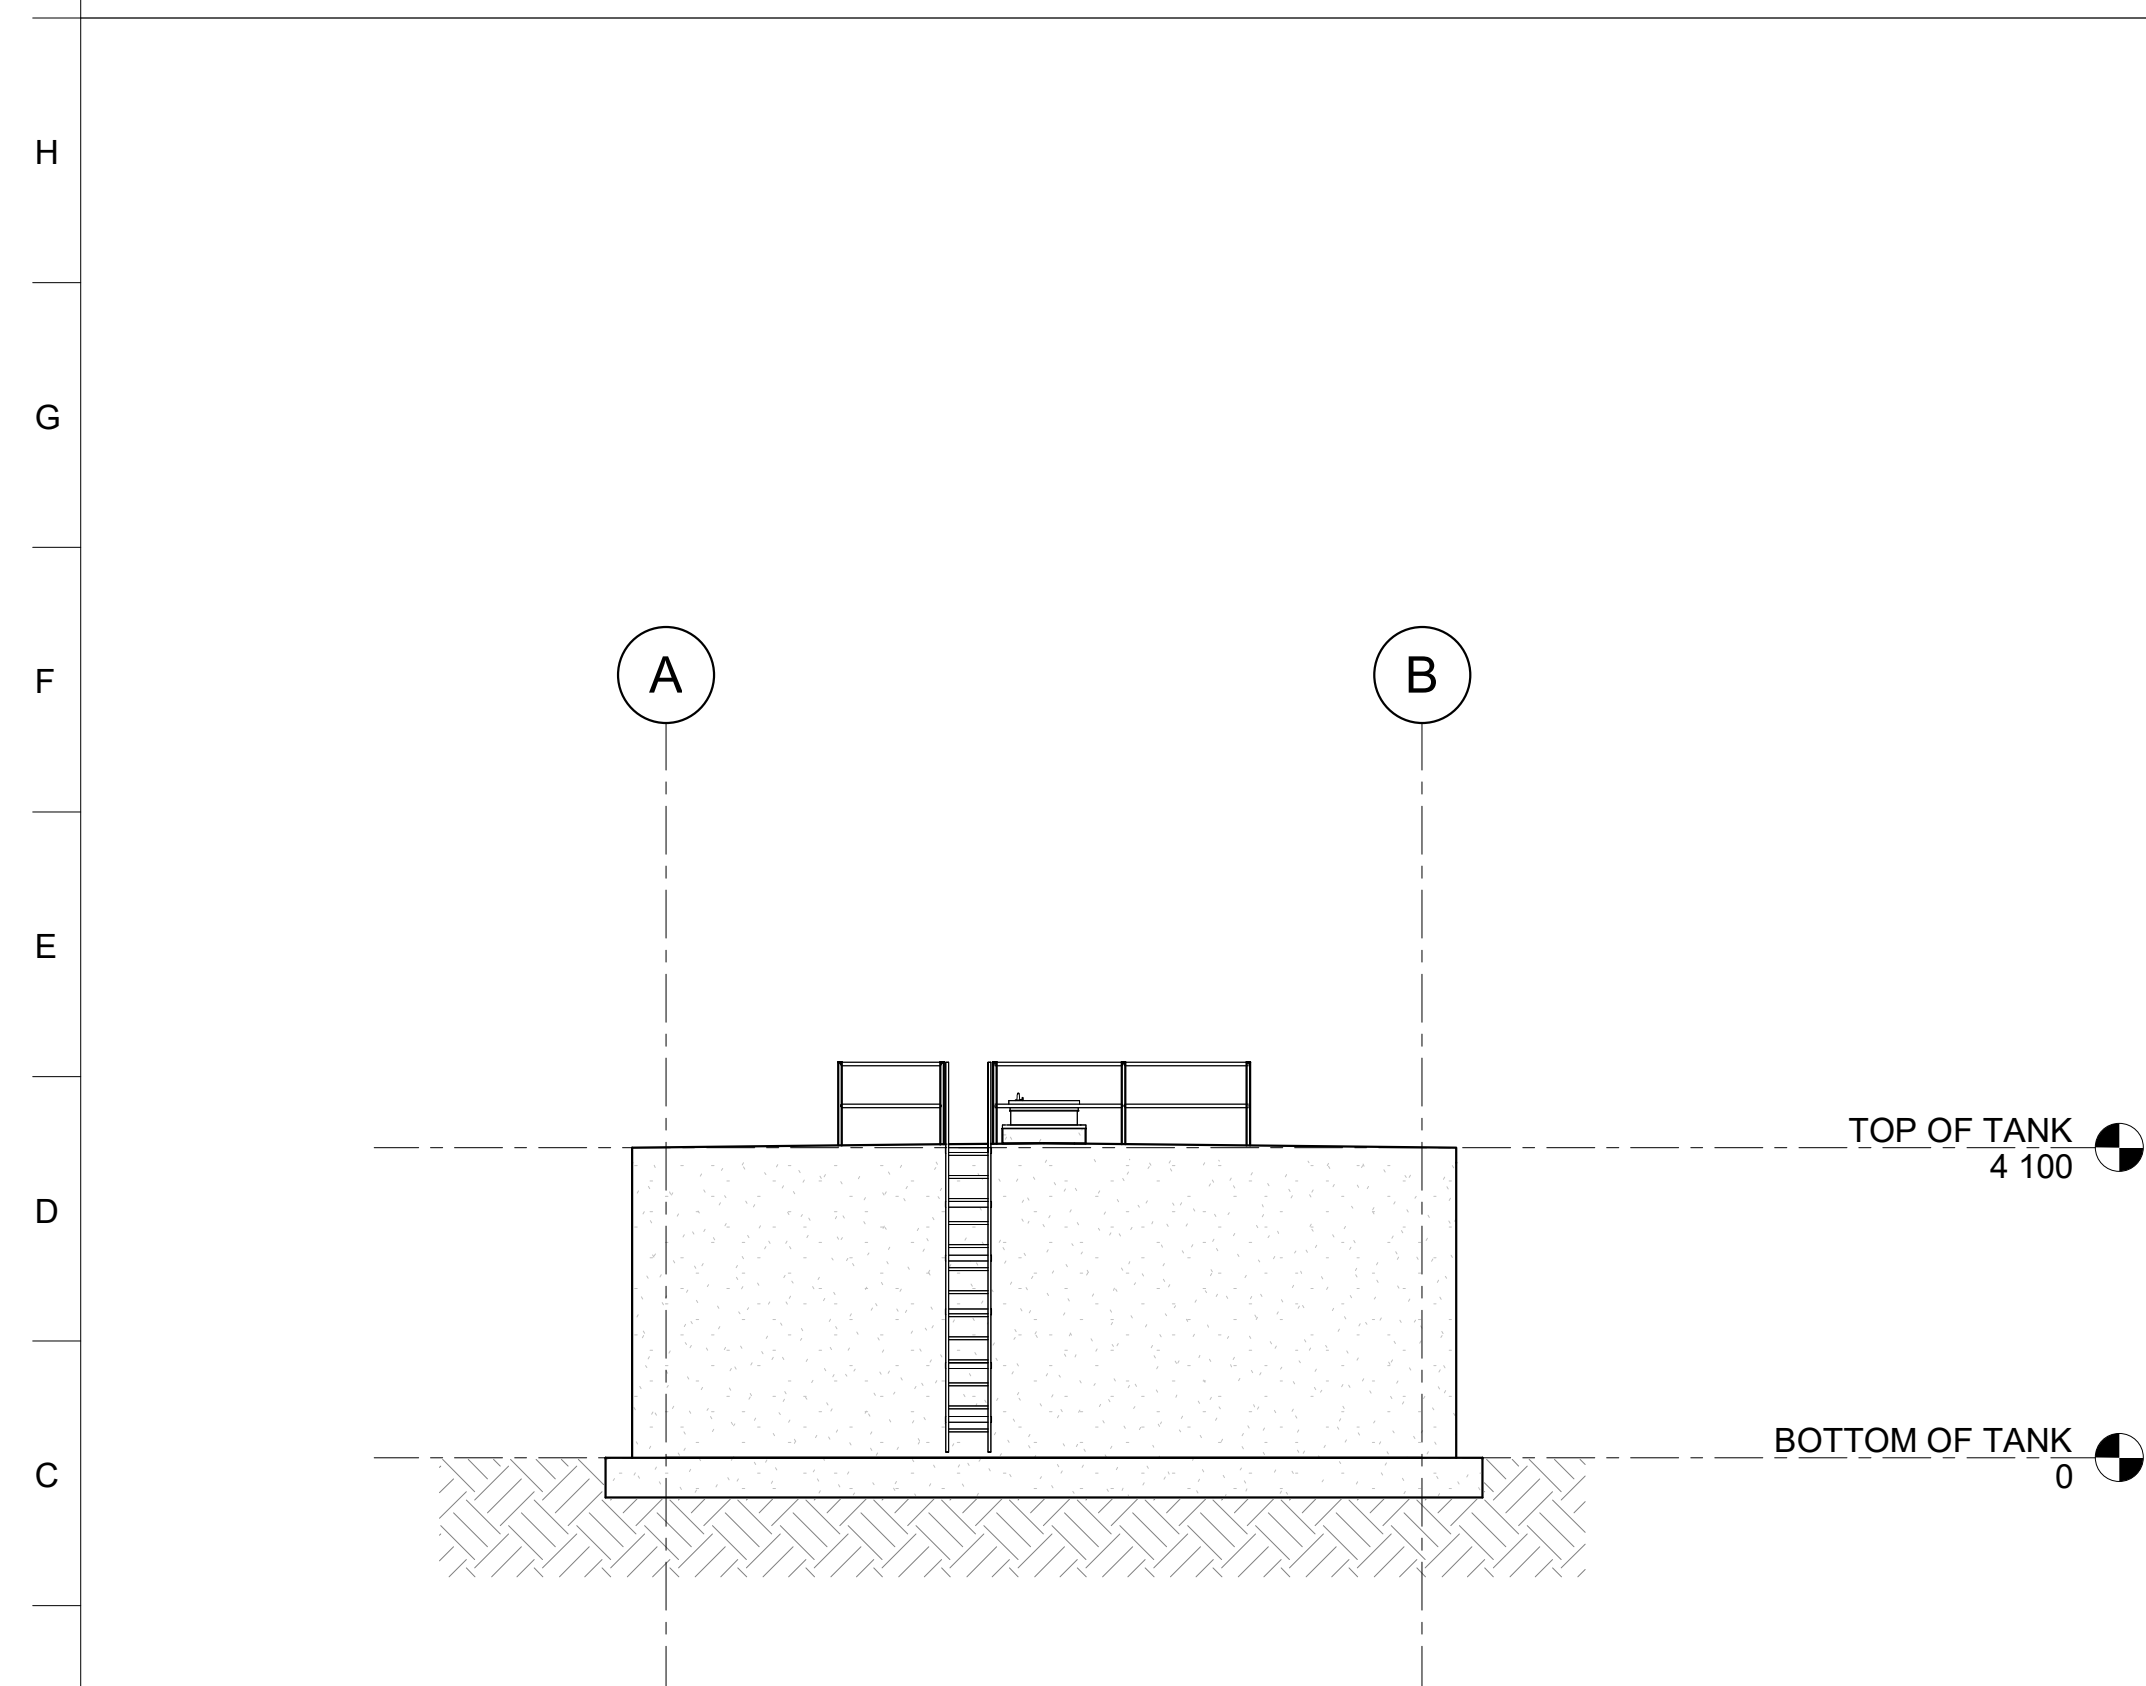

A1 WT - EXTERIOR ELEVATION WEST (CLIN 0001)
SCALE 1 : 100

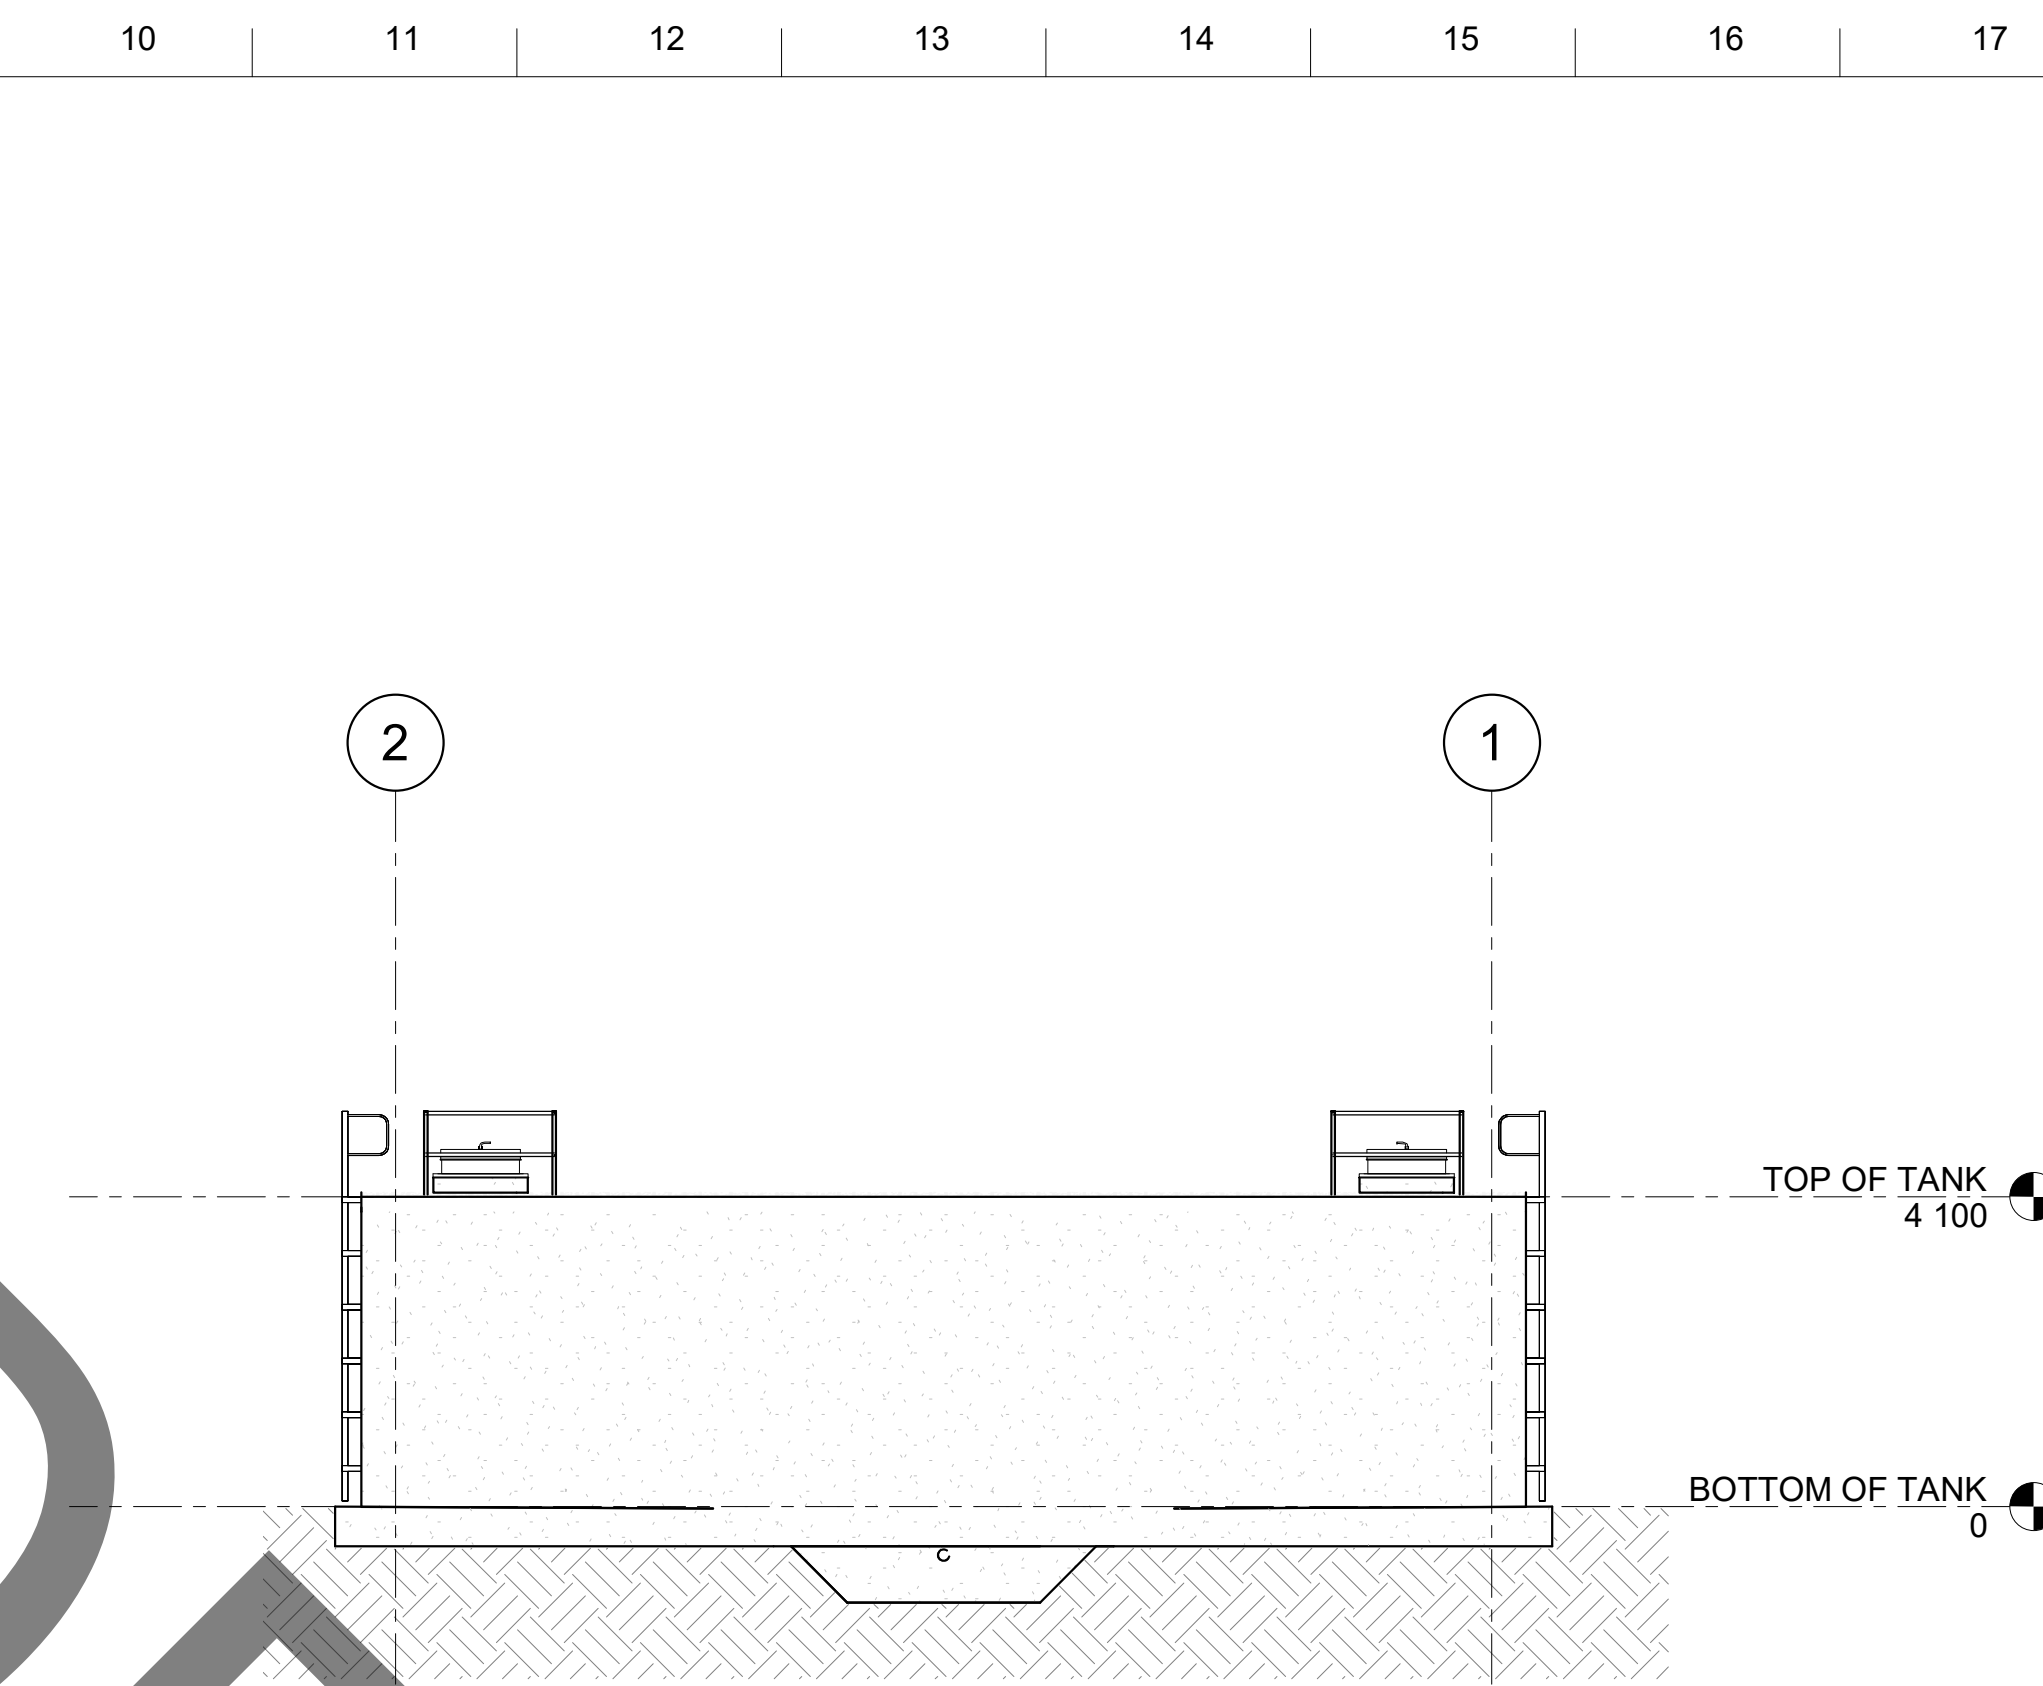

111 WT - EXTERIOR ELEVATION NORTH (CLIN 0001)
SCALE 1 : 100

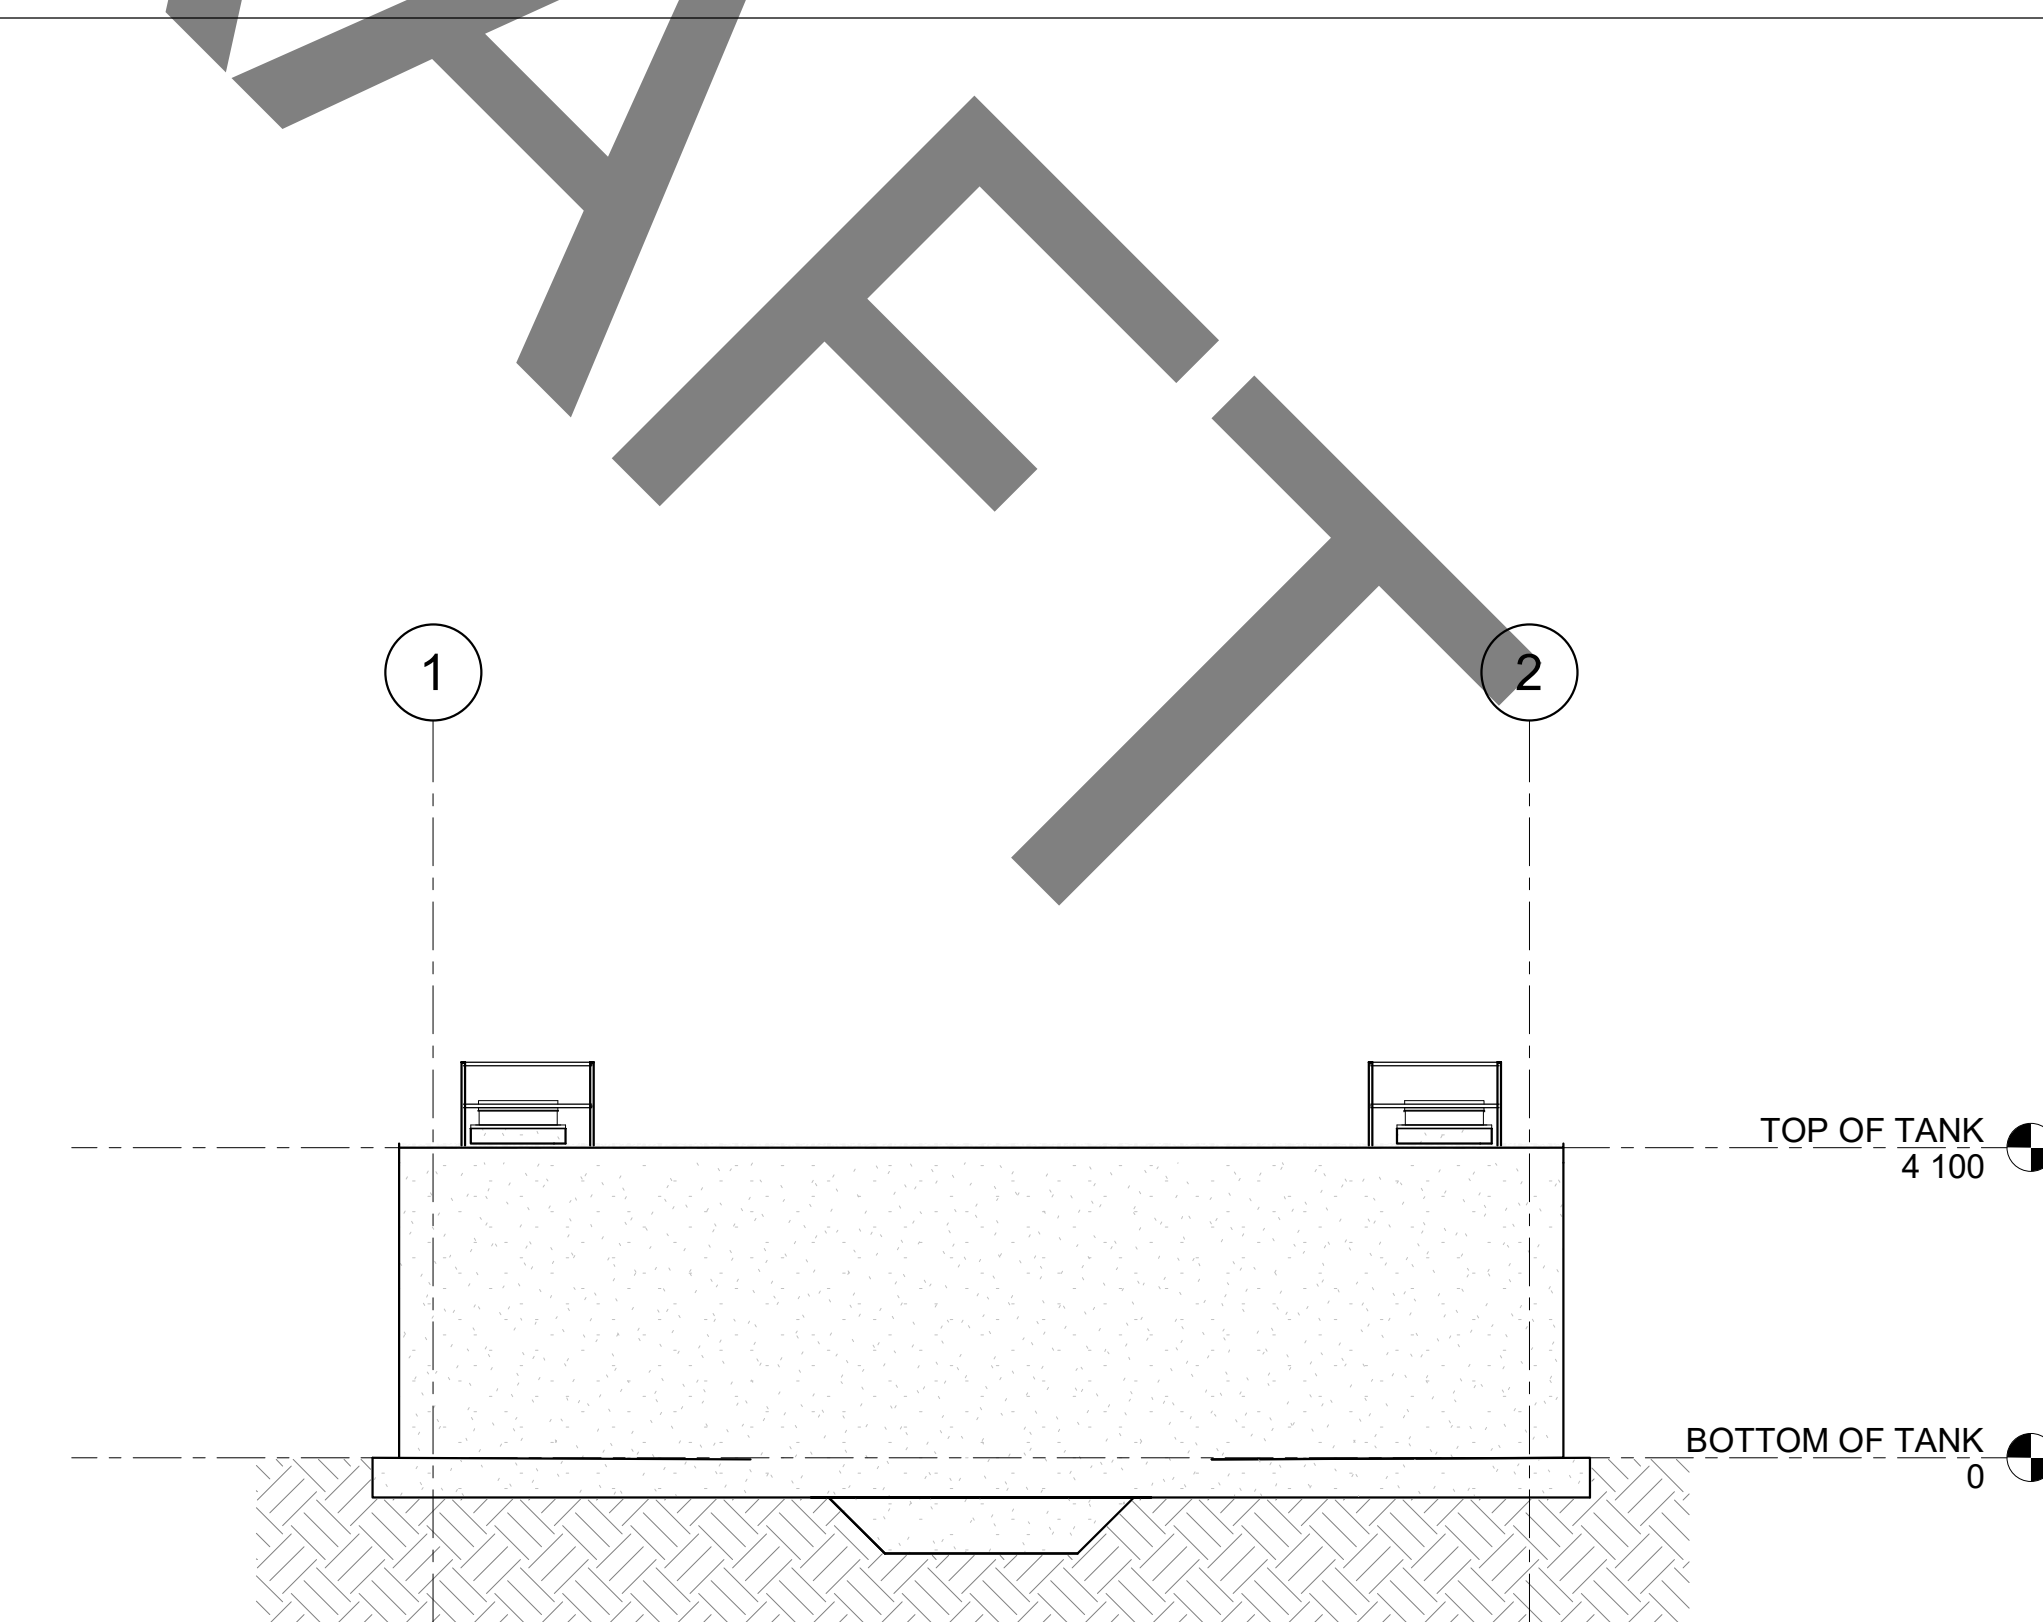

A11 WT - EXTERIOR ELEVATION SOUTH (CLIN 0001)
SCALE 1 : 100


REFERENCE DRAWINGS

S-001 - GENERAL NOTES
S-002 - DESIGN DATA, DESIGN CODES AND STANDARDS,
ABBREVIATION
S-501 - TYPICAL REINFORCING STEEL DETAILS
S-605 - CONCRETE WALL SCHEDULE
S-608 - CONCRETE BEAM DETAIL
S-609 - CONCRETE BEAM SCHEDULE

US Army Corps
of Engineers ®[illegible]

NOTES

1. SEE ARCHITECTURAL DRAWINGS FOR DIMENSIONS, ELEVATIONS AND DETAILS NOT SHOWN ON STRUCTURAL DRAWINGS.
2. SEE ARCHITECTURAL DRAWINGS FOR FLOOR SLOPE.
3. VERIFY WITH ARCHITECT/MECHANICAL FOR SIZE AND LOCATION OF OPENINGS.

 US ARMY CORPS OF ENGINEERS JAPAN ENGINEER DISTRICT OKINAWA AREA OFFICE APO AF 96376-5132	DESIGNED BY: DRAWN BY: R. TANGNONAN	ISSUE DATE: JUNE 2018 SOLICITATION NO.: CONTRACT NO.: W912HW-17-D-0003
	CHECKED BY: J. LUNO SUBMITTED BY: J. LUNO	
SSM INTERNATIONAL, INC. 501 SUMNER STREET, SUITE 620	SIZE:	

Autofeak Dns-Vehicle Maint Shm Kadana'S11758 TENE STIRIC nt

511-0-0-44

1	2	
---	---	---	---	---	---	---	---	---	----	----	-----

INTERMEDIATE DESIGN

APO AP 96343-5010
FY20 MCA PN77833 VEHICLE MAINTENANCE SHOP

WATER TANK - EXTERIOR ELEVATION (CLIN 0001)

SHEET ID
WT
S-I20

S-I201


CLIN 0001

GRAPHIC SCALE

0 2000 4000

SCALE: 1 : 100

ALL DIMENSIONS AND/OR DIMENSIONS SHOWN IN
CALLOUT/ NOTES ARE IN MILLIMETERS UNLESS
NOTED OTHERWISE.

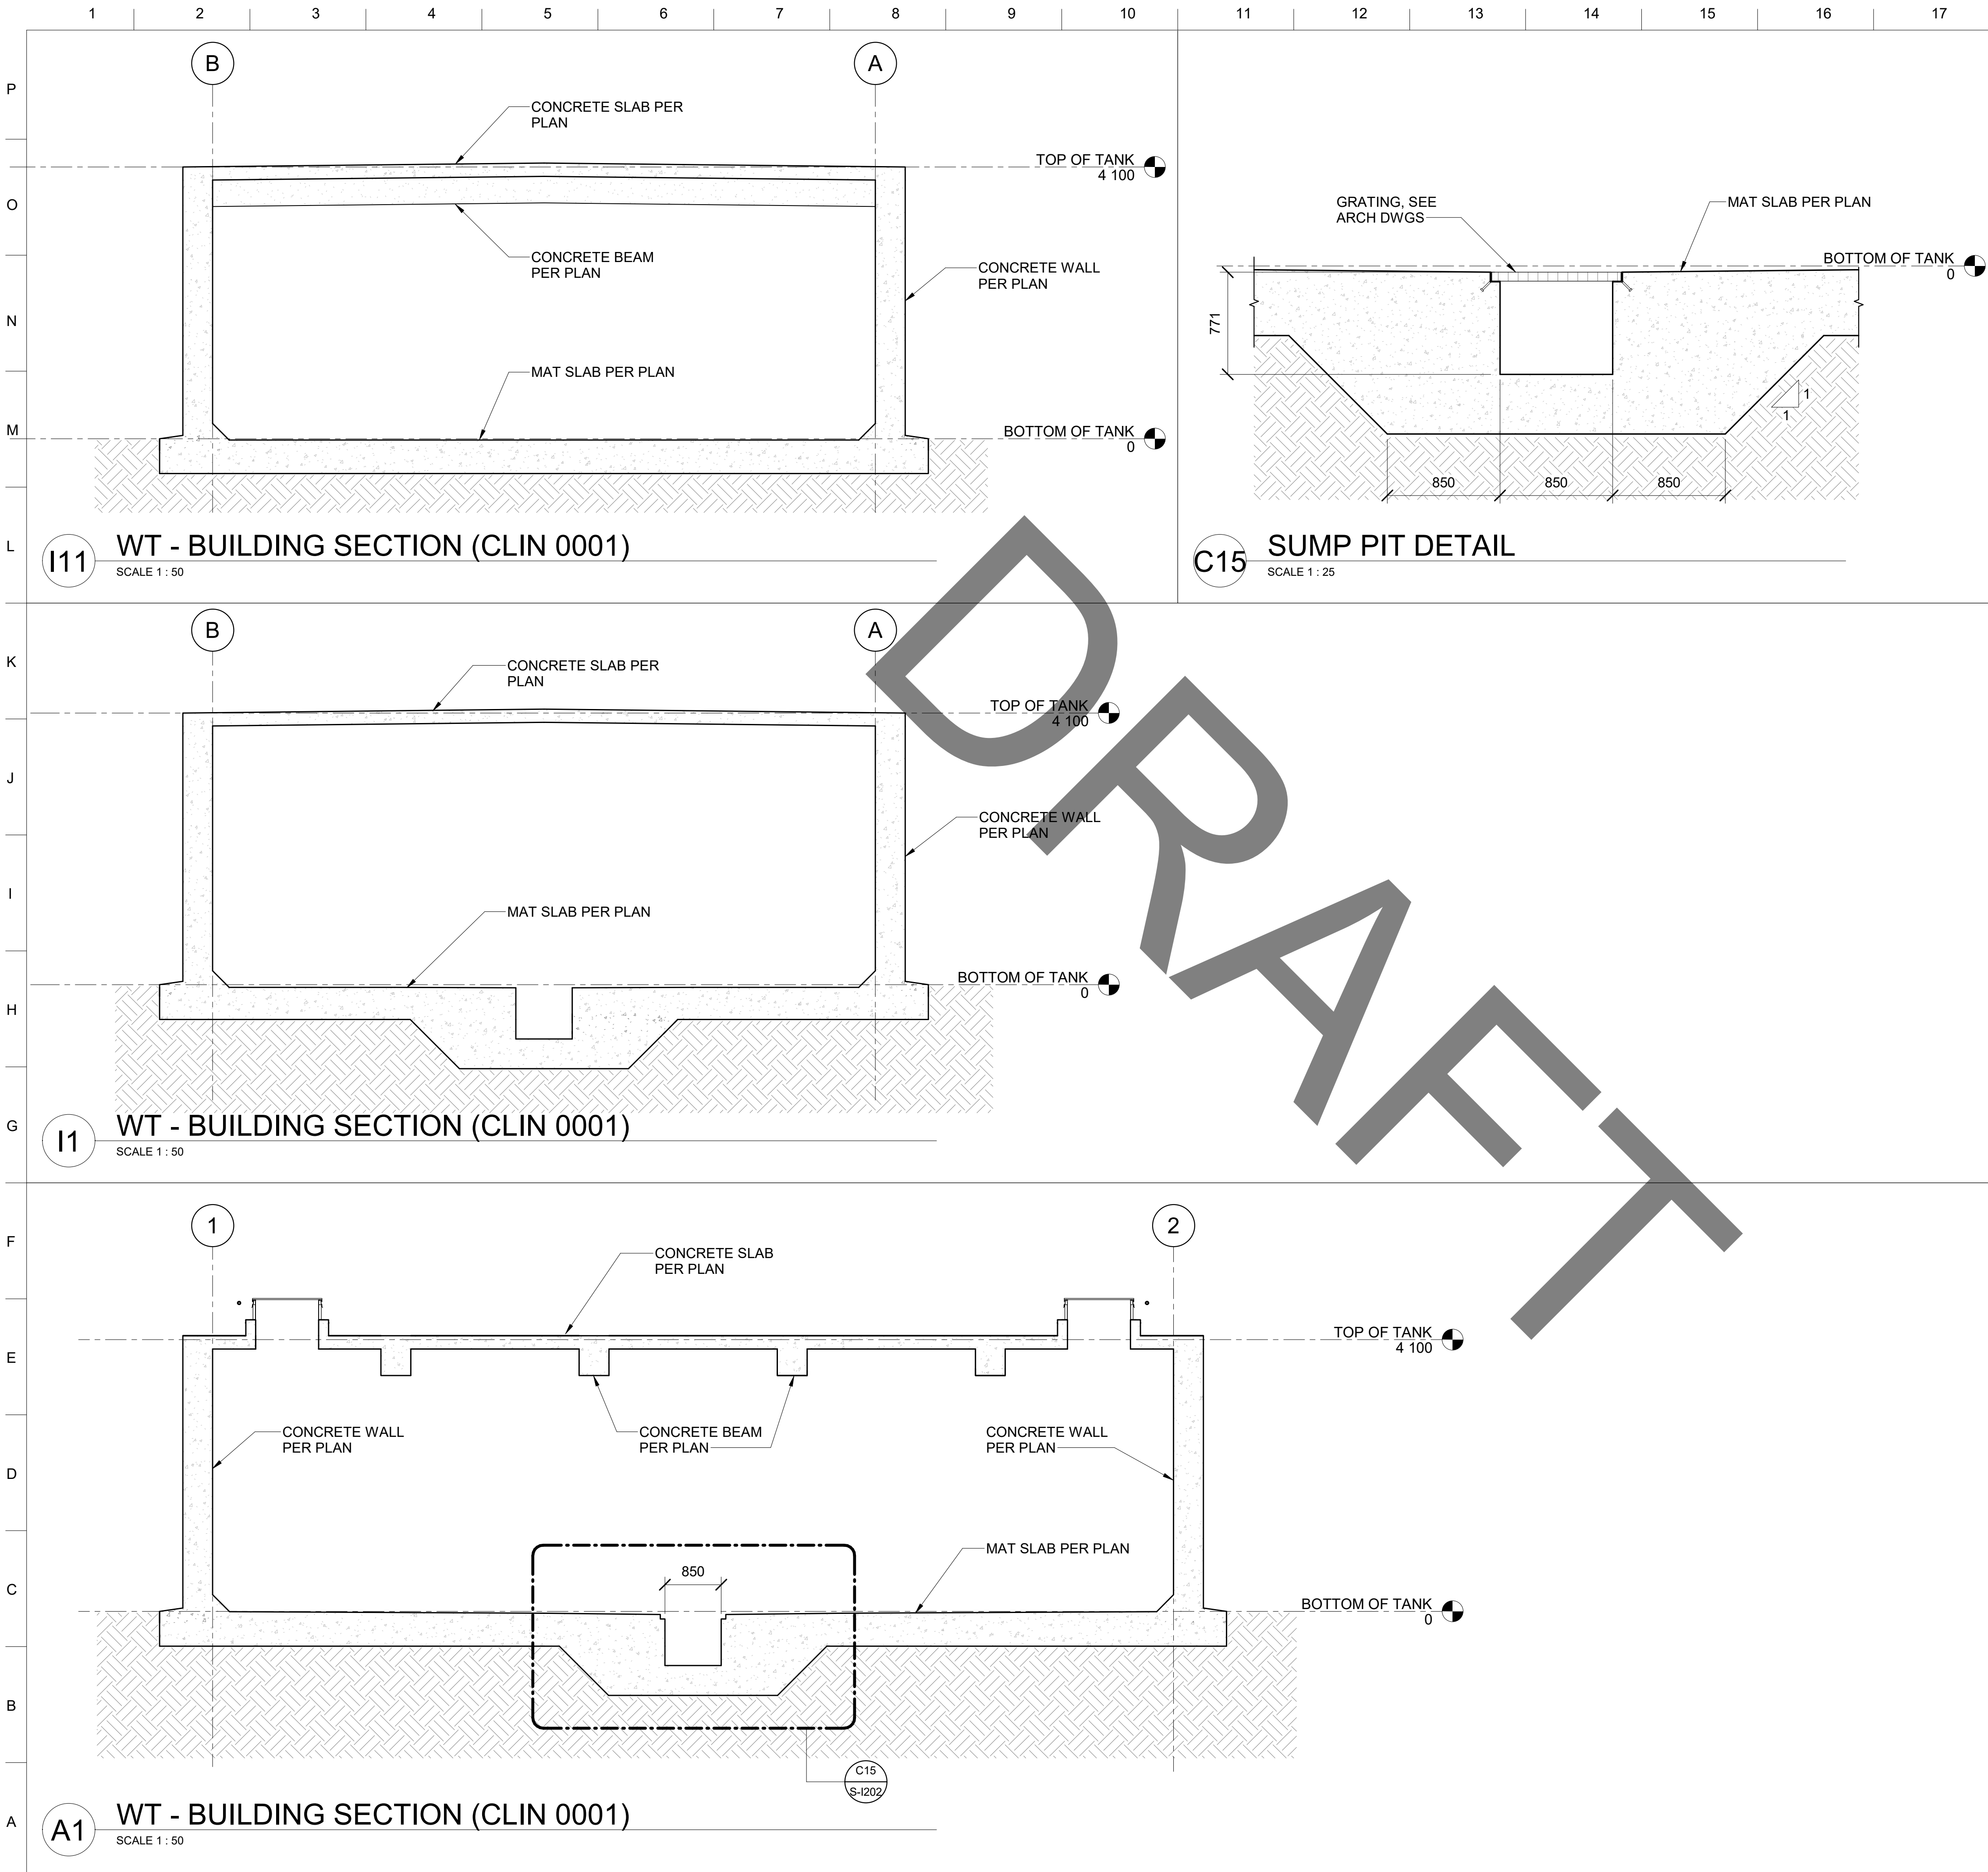

REFERENCE DRAWINGS

S-001 - GENERAL NOTES
S-002 - DESIGN DATA, DESIGN CODES AND STANDARDS, ABBREVIATION
S-501 - TYPICAL REINFORCING STEEL DETAILS
S-605 - CONCRETE WALL SCHEDULE
S-608 - CONCRETE BEAM DETAIL
S-609 - CONCRETE BEAM SCHEDULE

NOTES

1. SEE ARCHITECTURAL DRAWINGS FOR DIMENSIONS, ELEVATIONS AND DETAILS NOT SHOWN ON STRUCTURAL DRAWINGS.

2. SEE ARCHITECTURAL DRAWINGS FOR FLOOR SLOPE.

3. VERIFY WITH ARCHITECT/MECHANICAL FOR SIZE AND LOCATION OF OPENINGS.

CLIN 0001

GRAPHIC SCALE

PLAN NORTH

GRAPHIC SCALE

SCALE: 1 : 100

ALL DIMENSIONS AND/OR DIMENSIONS SHOWN IN CALLOUT/NOTES ARE IN MILLIMETERS UNLESS NOTED OTHERWISE.

US Army Corps of Engineers®

ISSUE DATE:
JUNE 2018

DESIGNED BY:
J. RABANAL

DRAWN BY:
R. TANGONAN

CHECKED BY:
J. UNO

SUBMITTED BY:
J. UNO

SIZE:
ANSI D

SOLICITATION NO.:
W912AV-17-D-0003

CONTRACT NO.:
W912AV-17-D-0003

US ARMY CORPS OF ENGINEERS
JAPAN ENGINEER DISTRICT
OKINAWA AREA OFFICE
APO AP 96376-5132

SSFM

SSFM INTERNATIONAL, INC.
501 SUMNER STREET, SUITE 620
HONOLULU, HAWAII 96817

DATE

DESCRIPTION

MARK

APO AP 96343-5010
FY20 MCA PN77833 VEHICLE MAINTENANCE SHOP

WATER TANK - BUILDING SECTIONS (CLIN 0001)

SHEET ID
WT
S-I202

INTERMEDIATE DESIGN


Plot Date: 12/16/2025 3:38:13 PM File Path: AutoDesk Docs/Vehicle Maint Shop/Kadena/S-I202_TEMP.STRUC.rvt

NTS




1 2 3 4 5 6 7 8 9 10 11 12 13 14 15 16 17 18 19 20 21


P
O
N
M
L
K
J
I
H
G
F
E
D
C
B
A

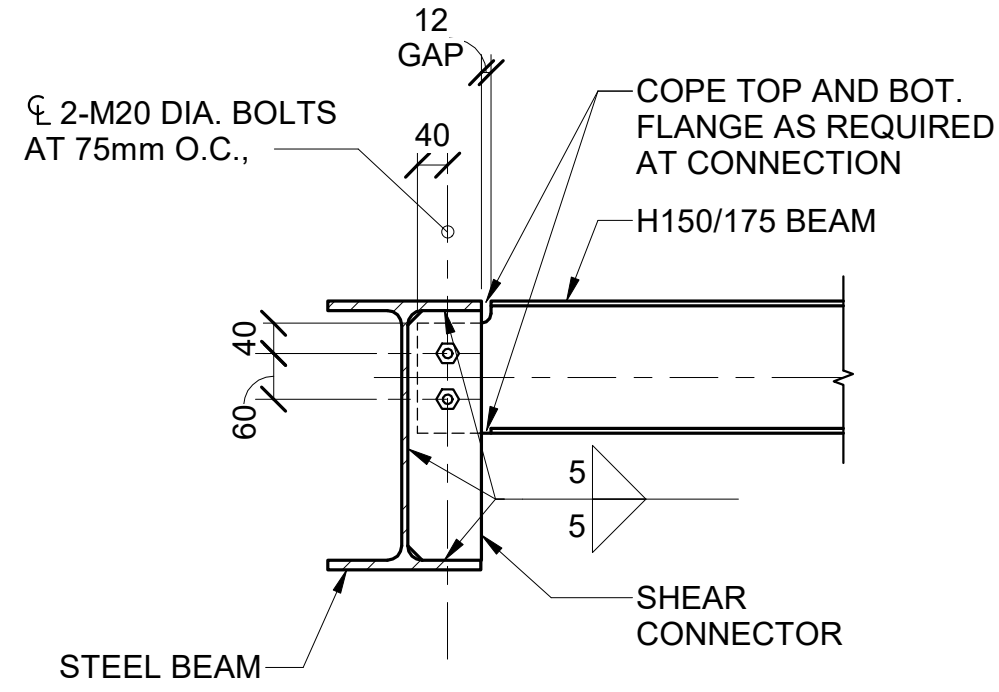


CONDITION AT H150 OR H175 BEAM

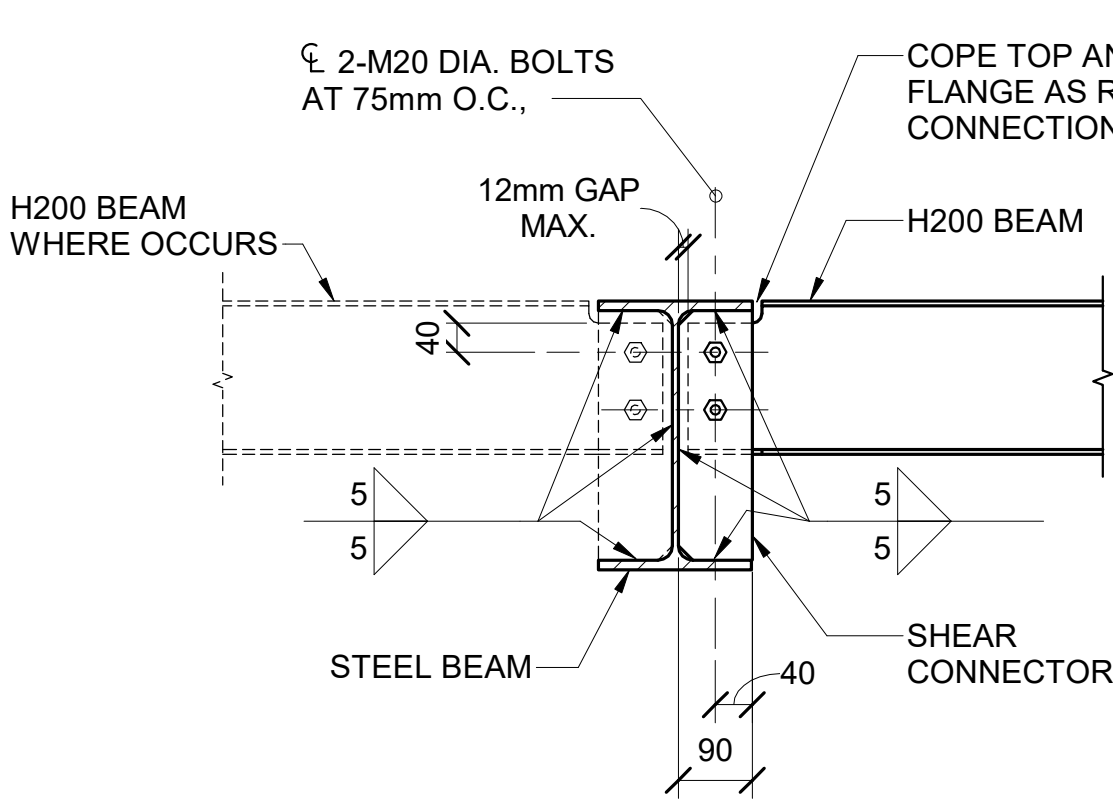


CONDITION AT H200 AND H250 BEAM

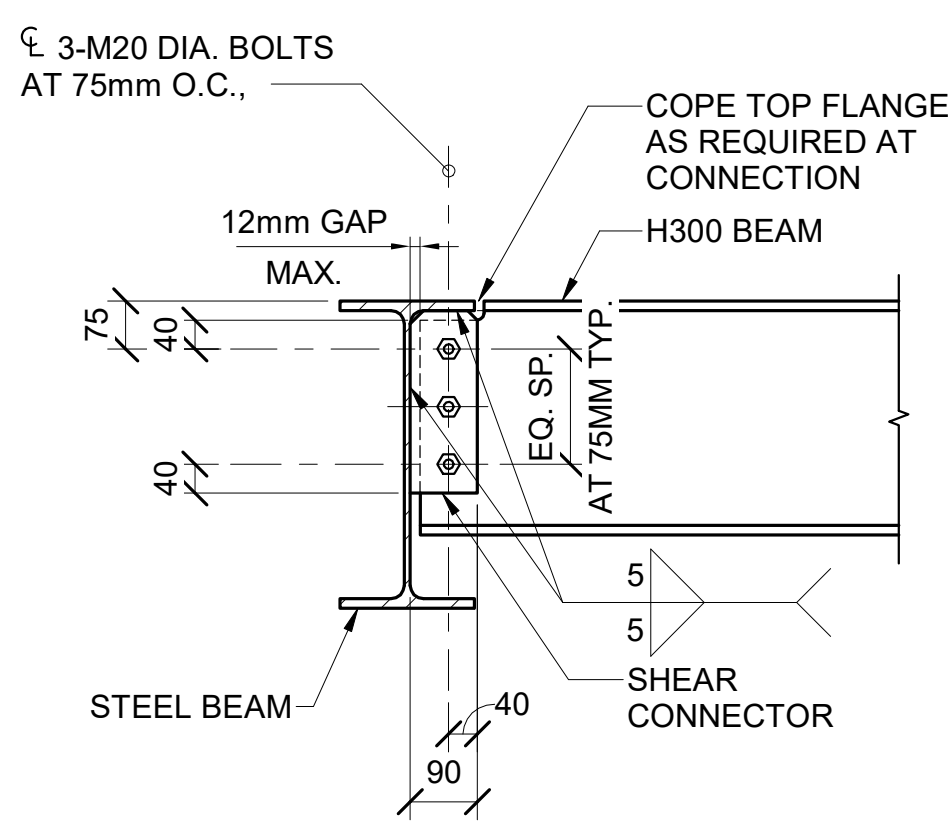


CONDITION AT H300 BEAM

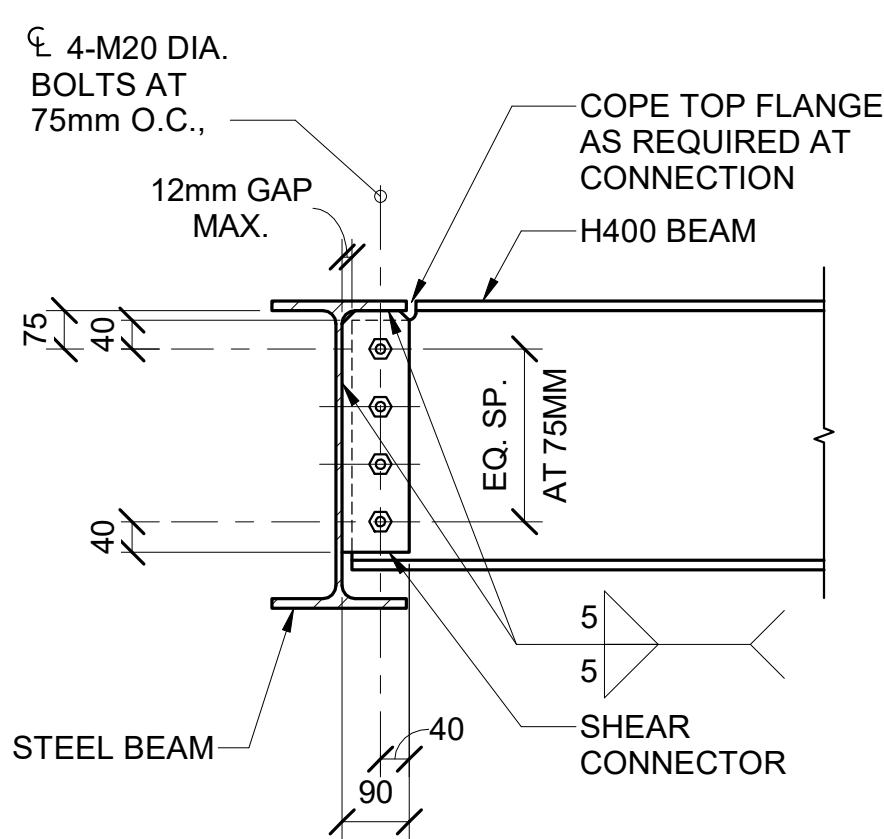

CONDITION AT H400 BEAM

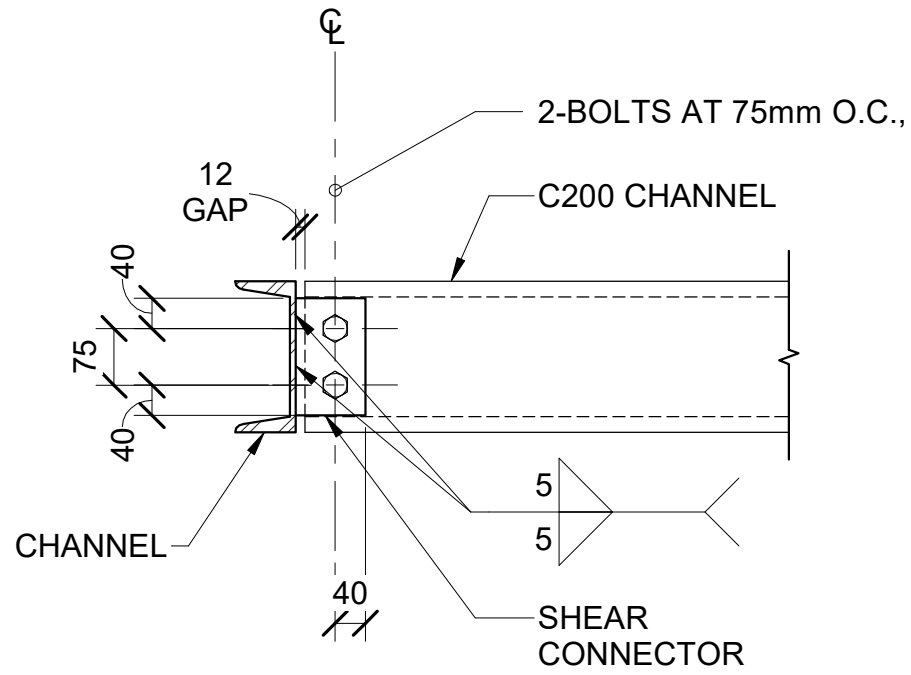

CHANNEL TO CHANNEL CONNECTION

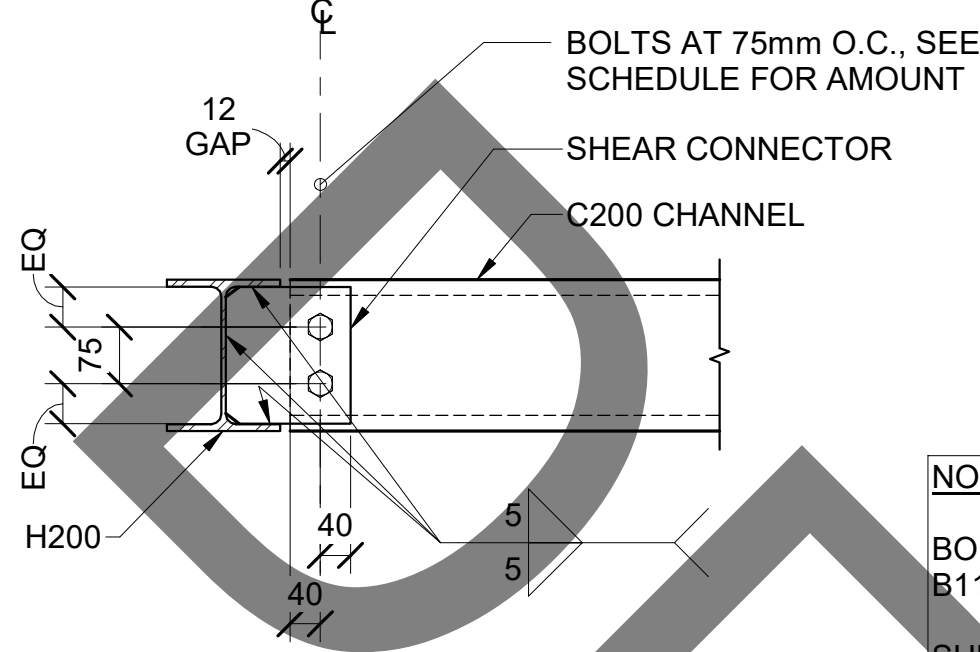


CHANNEL TO BEAM CONNECTION


NOTE:
BOLTS MUST BE ASTM A325 OR JIS B1186, F10T.
SHEAR PLATE MUST BE 9mm THICK

14 TYPICAL STEEL BEAM CONNECTION DETAILS


STRUCTURAL STEEL SECTION SCHEDULE		
MARK	WEB THICKNESS (mm)	FLANGE THICKNESS (mm)
H800X300	14	26
H400X300	10	16
H400X200	8	13
H300X300	10	15
H250X250	9	14
RF-1 H700X300	13	24
H300X150	6.5	9
H200X200	8	12

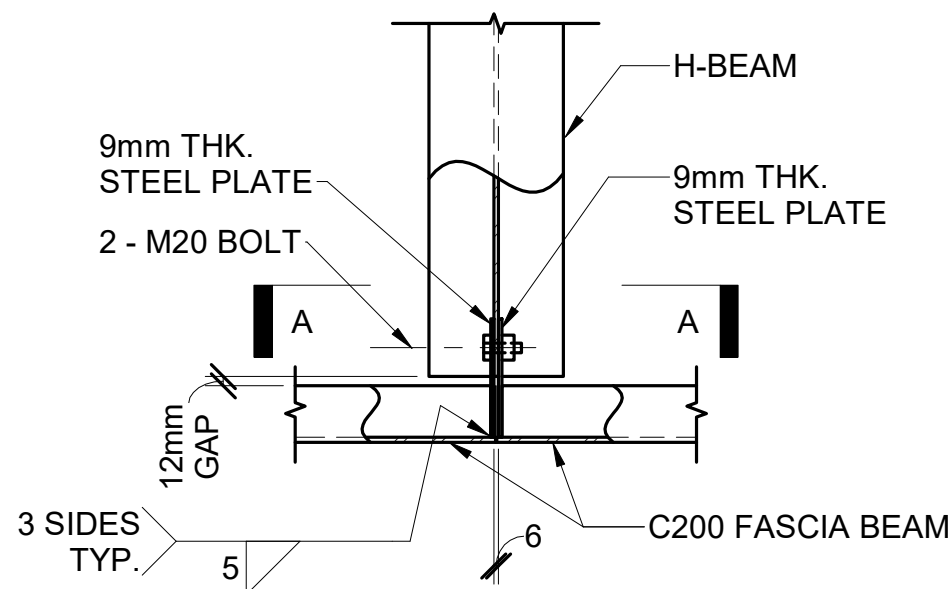


PLAN

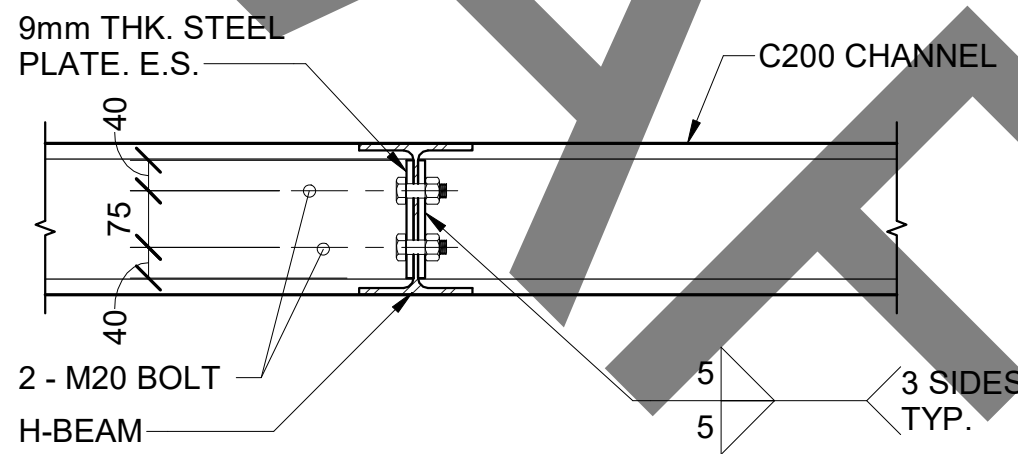

SECTION A - A

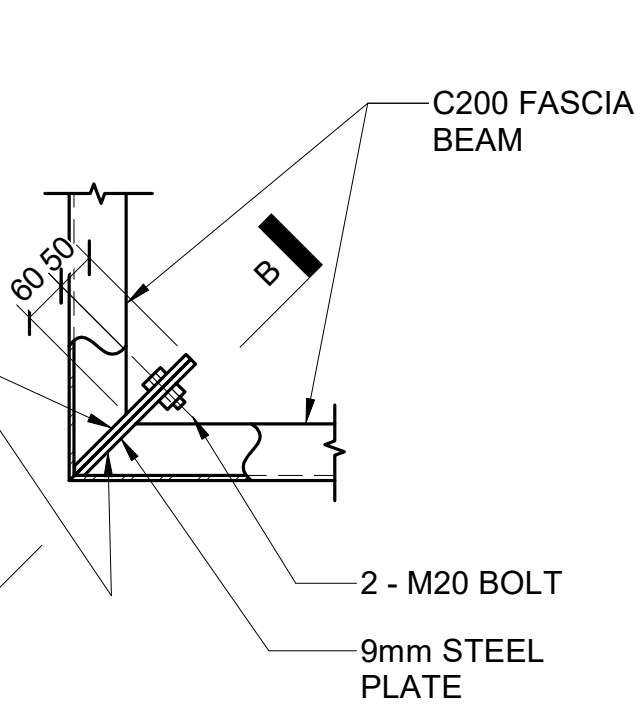


PLAN

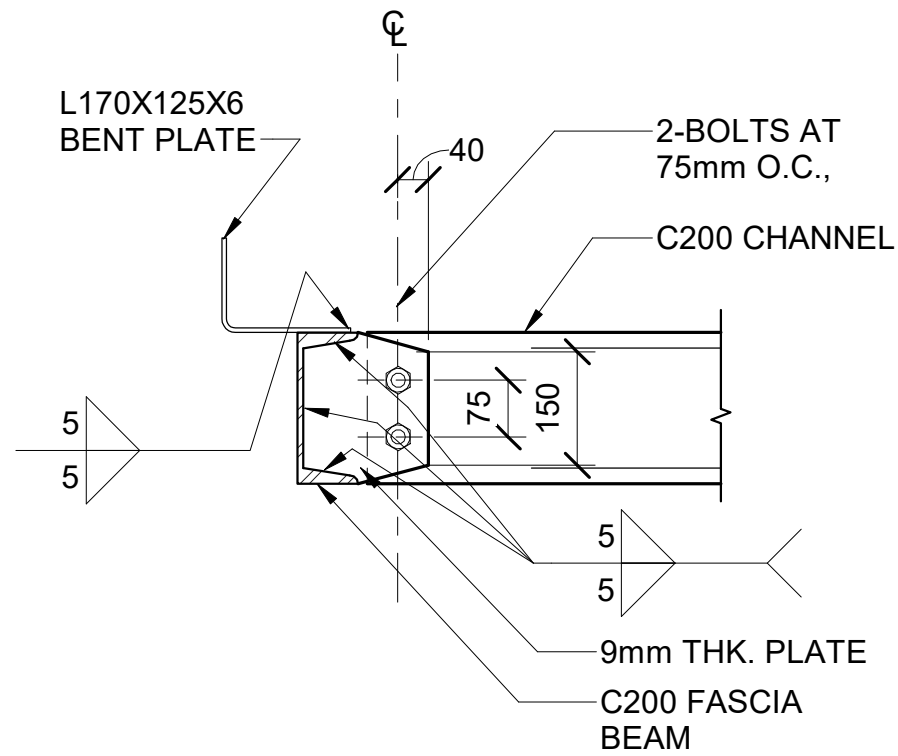


SECTION B - B

TYPICAL FASCIA BEAM SPLICE DETAIL


TYPICAL FASCIA TO FASCIA CORNER DETAIL

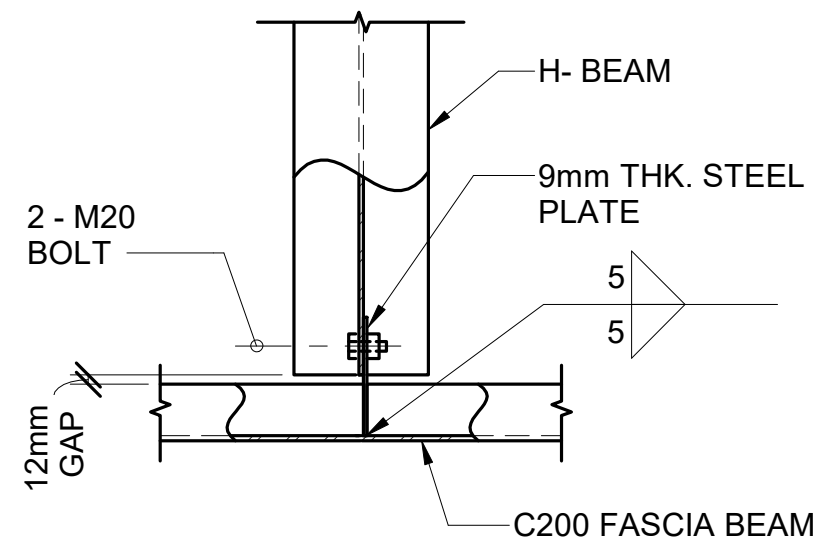


PLAN

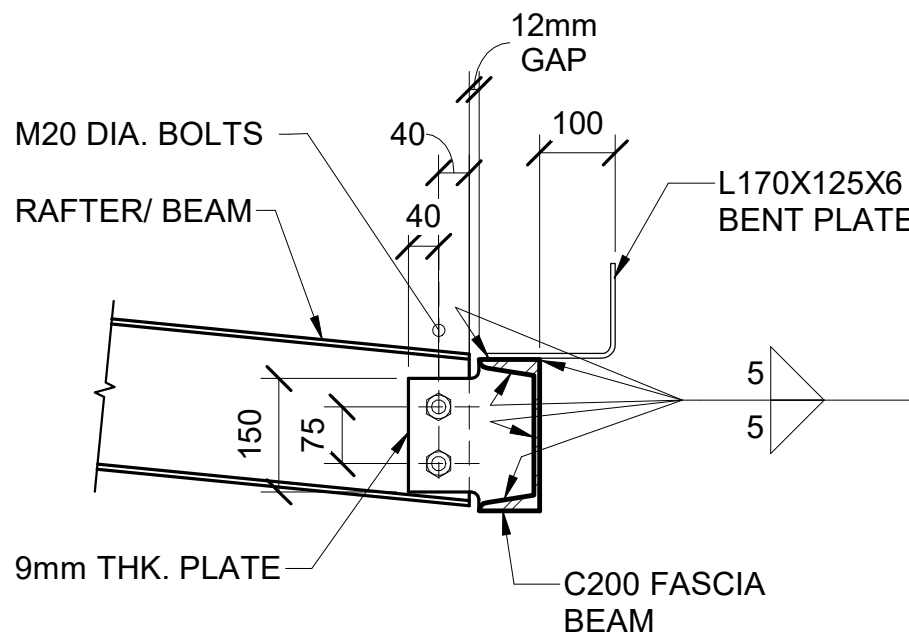

CONDITION AT H175/H200 STEEL RAFTER/B EAM

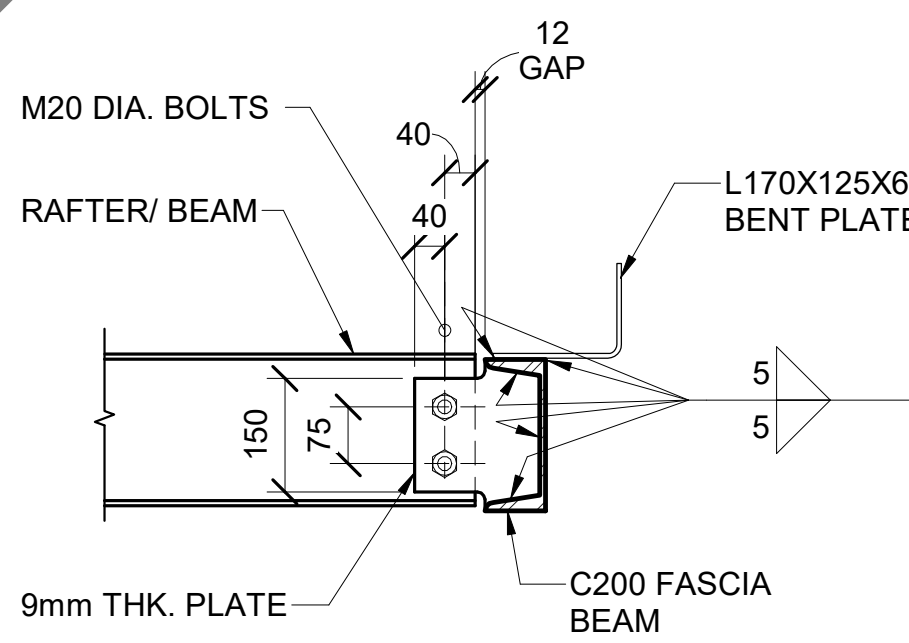

TYPICAL C200 FASCIA TO BEAM CONNECTION DETAIL

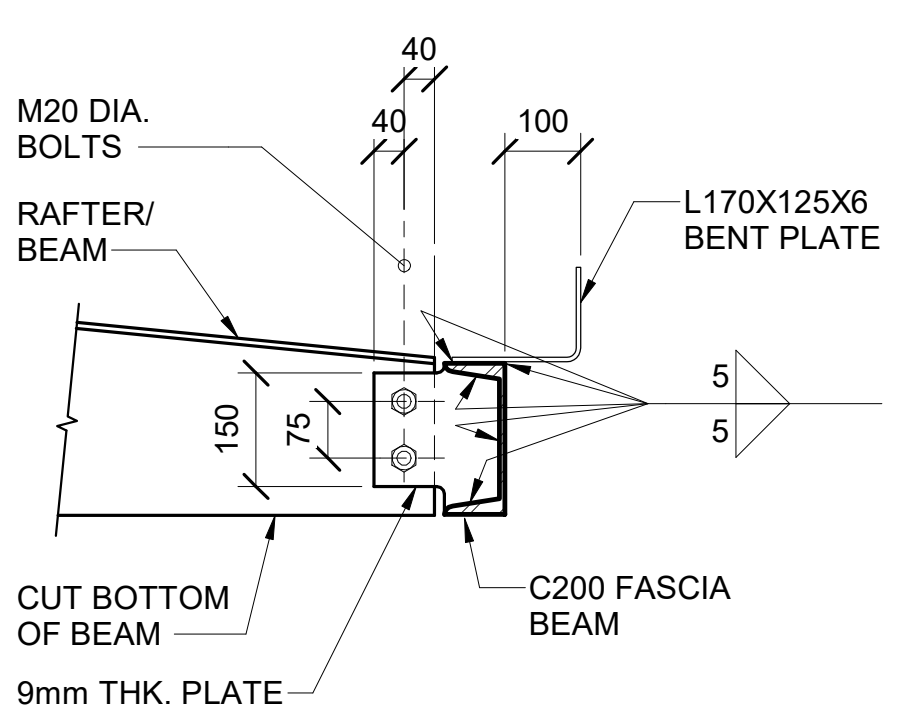

CONDITION AT H250/H300/H400 STEEL RAFTER/B EAM

A1 TYPICAL STEEL SECTION SCHEDULE

A10 TYPICAL FASCIA CONNECTION DETAILS

US Army Corps of Engineers




ISSUE DATE:	DESIGNED BY:	U.S. ARMY CORPS OF ENGINEERS
JUNE 2018	J. RABANAL	JAPAN ENGINEER DISTRICT
SOLICITATION NO.:	R. TANGONAN	OKINAWA AREA OFFICE
CONTRACT NO.:	W912RY-17-D-0003	SSFM INTERNATIONAL, INC.
DATE:	J. UNO	501 SUMNER STREET, SUITE 620
DESCRIPTION:	SIZE: ANS I D	HONOLULU, HAWAII 96817
MARK:		


APO AP 96343-5010
FY20 MCA PN7833 VEHICLE MAINTENANCE SHOP


TYPICAL STEEL NOTES AND DETAILS

SHEET ID













S-504

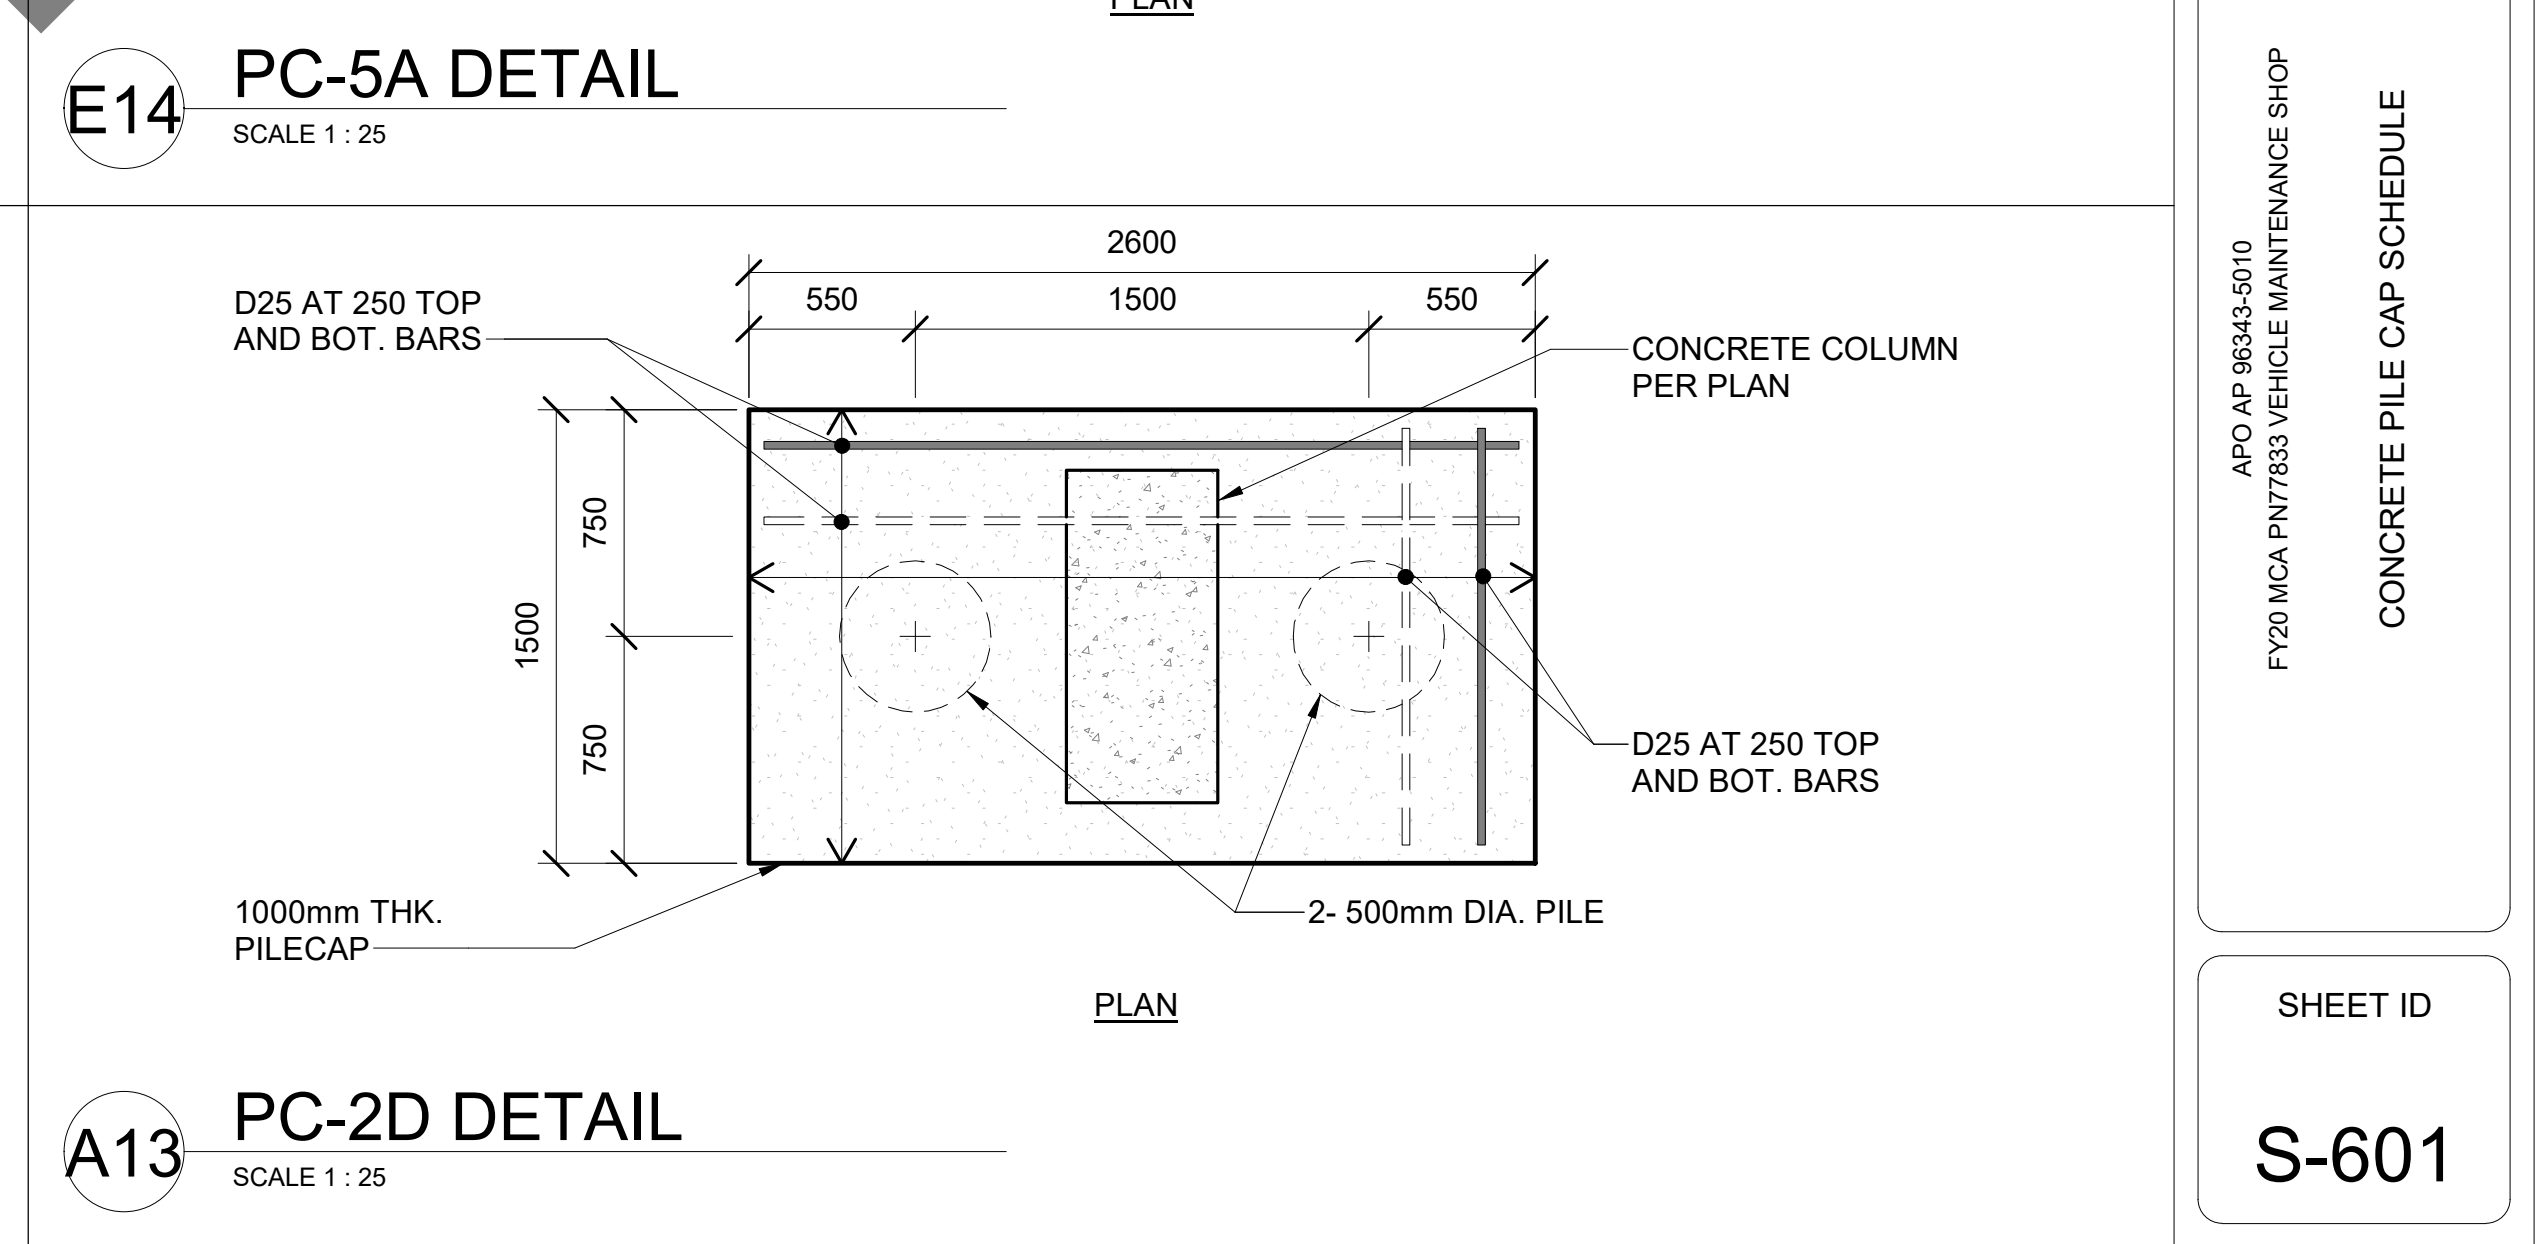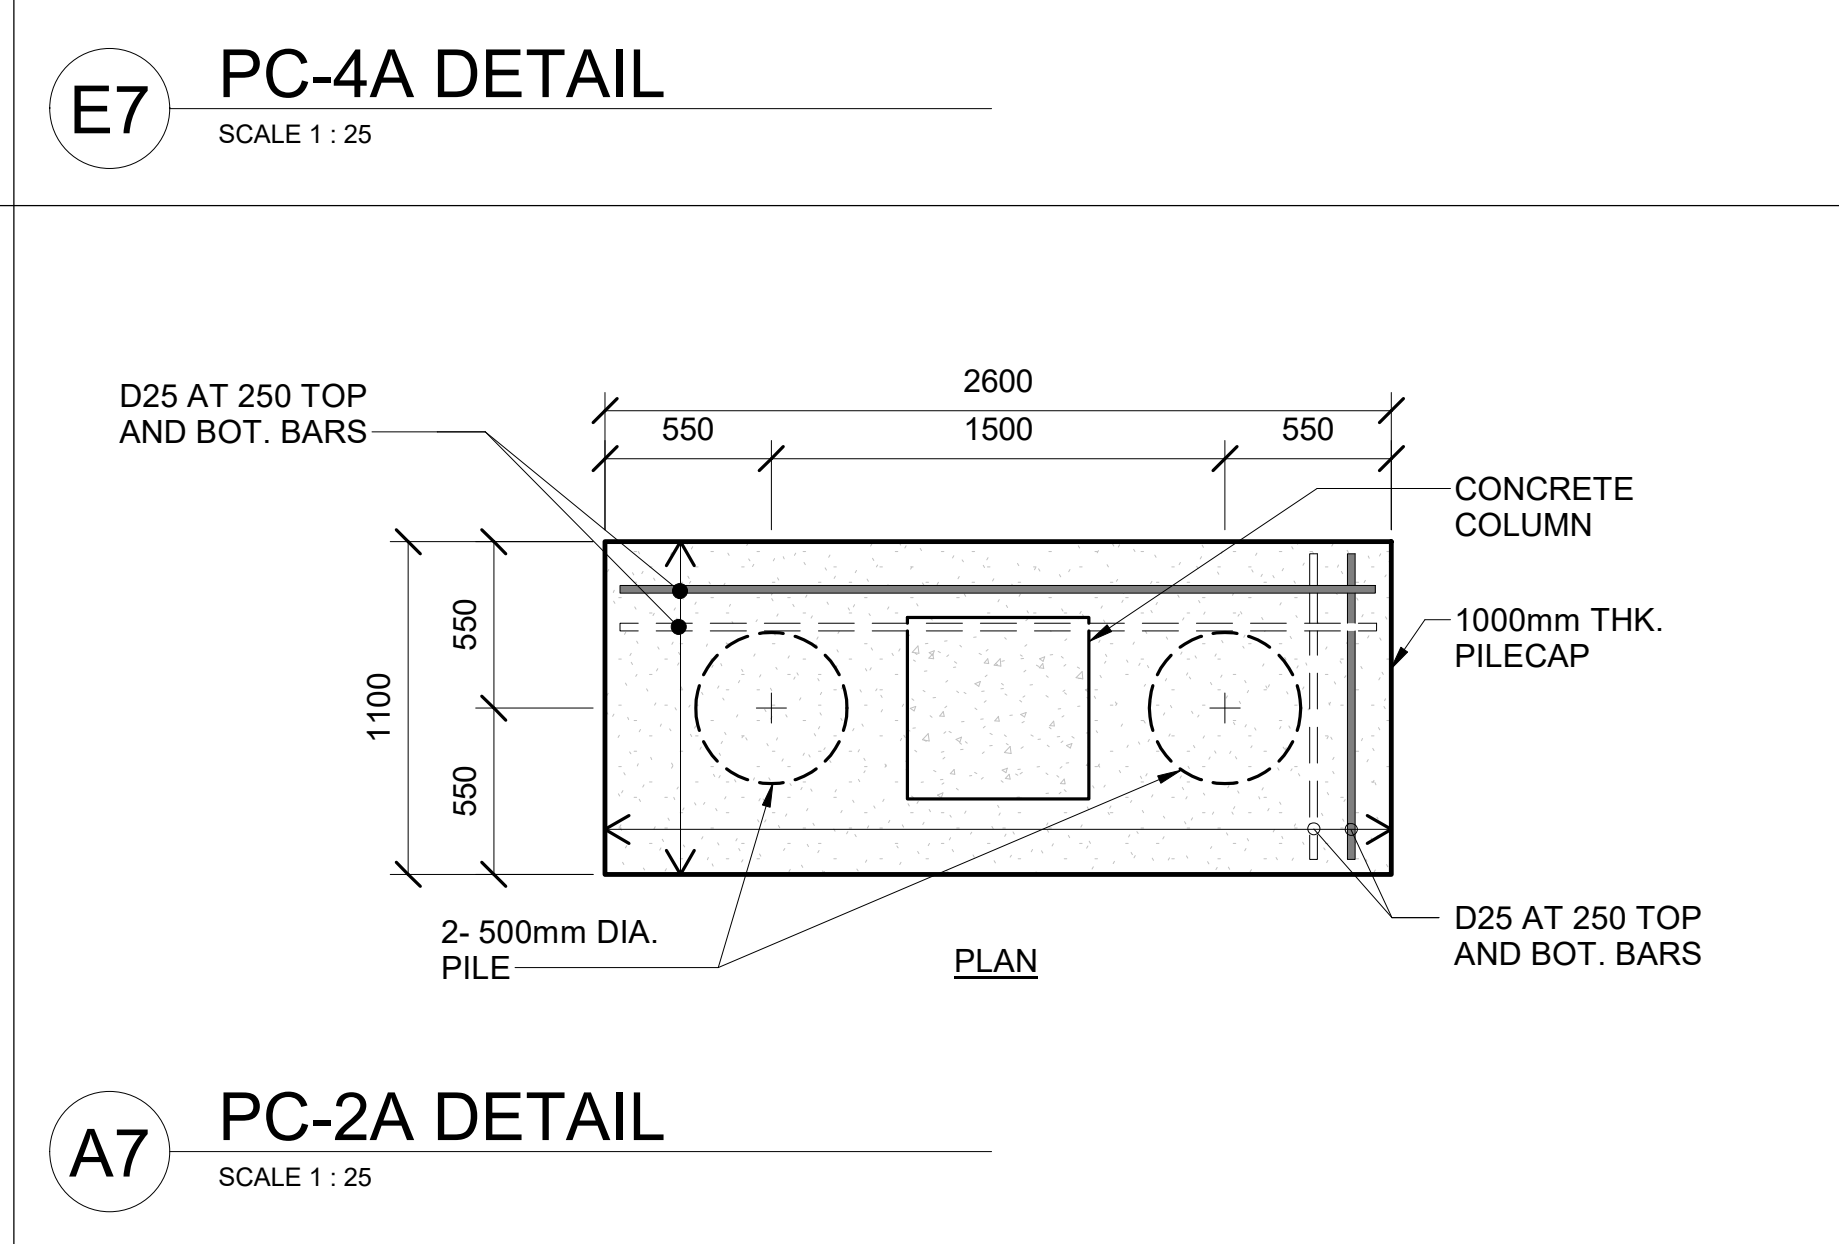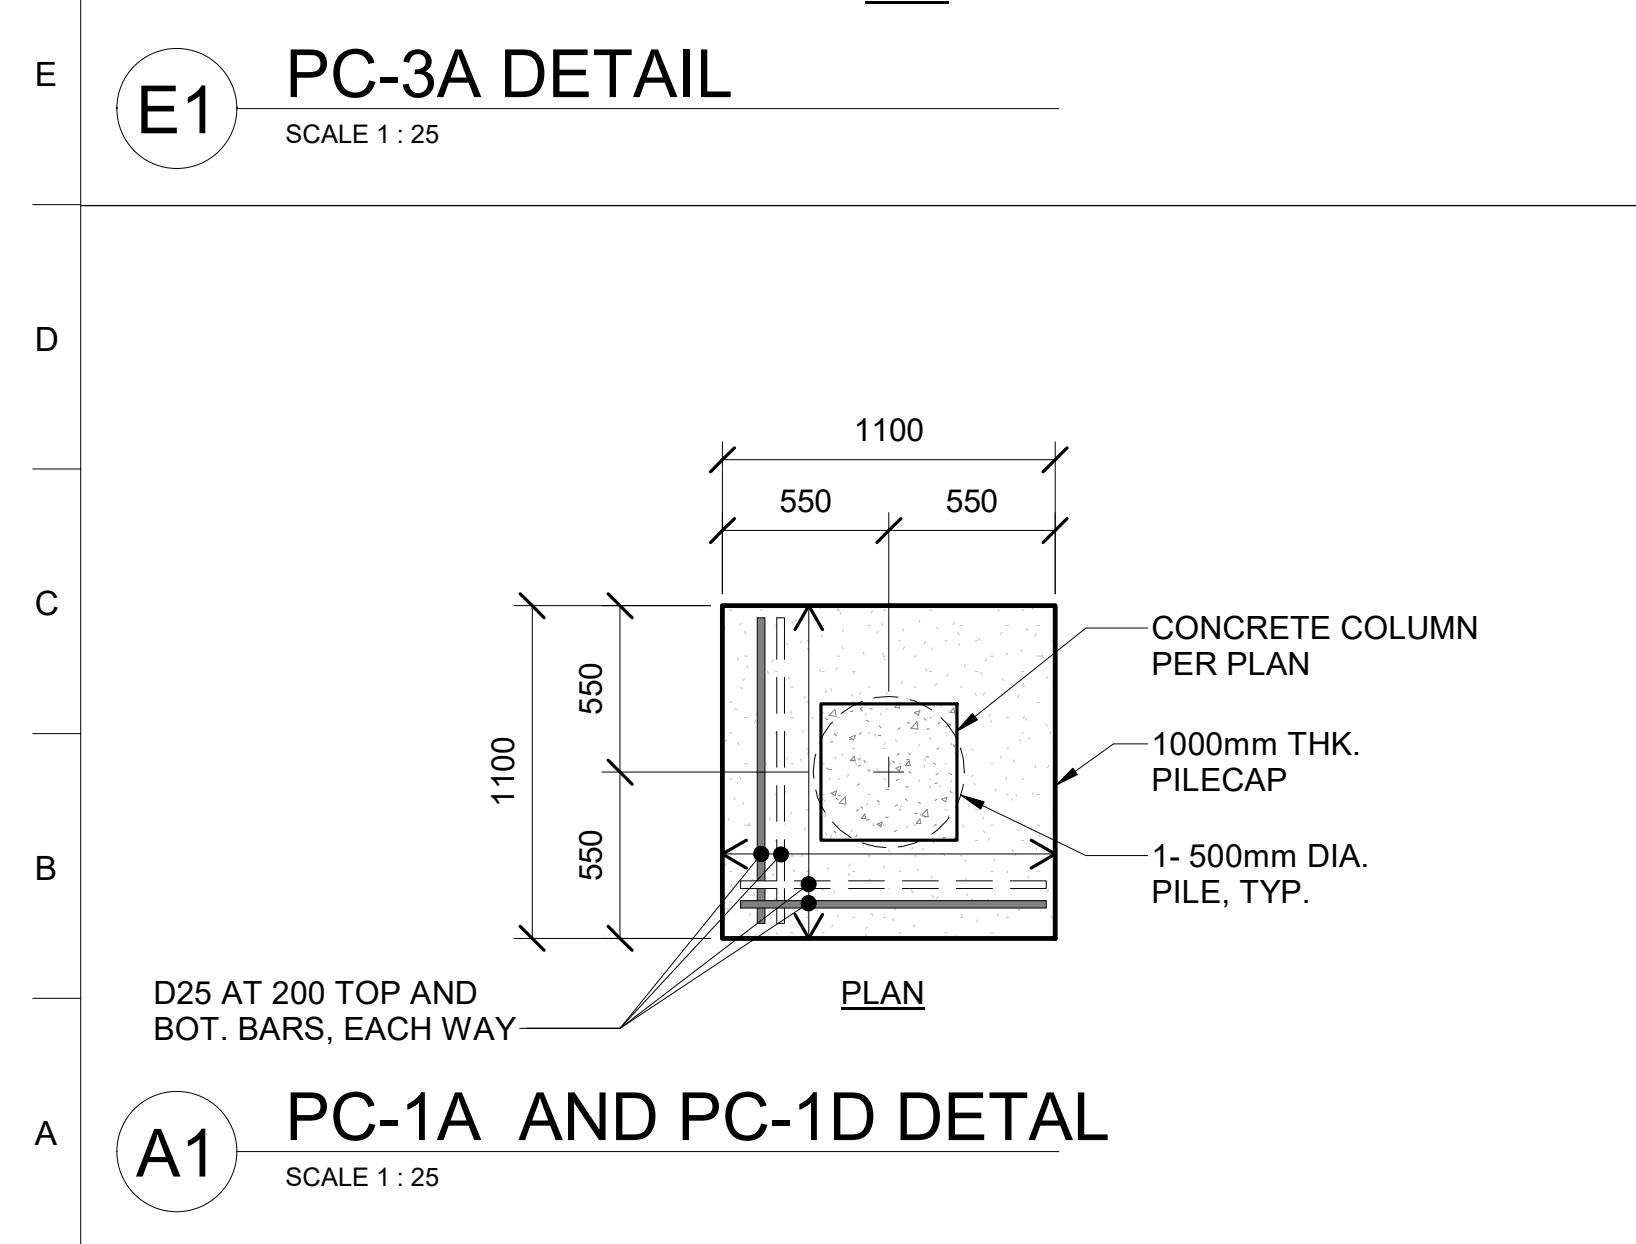

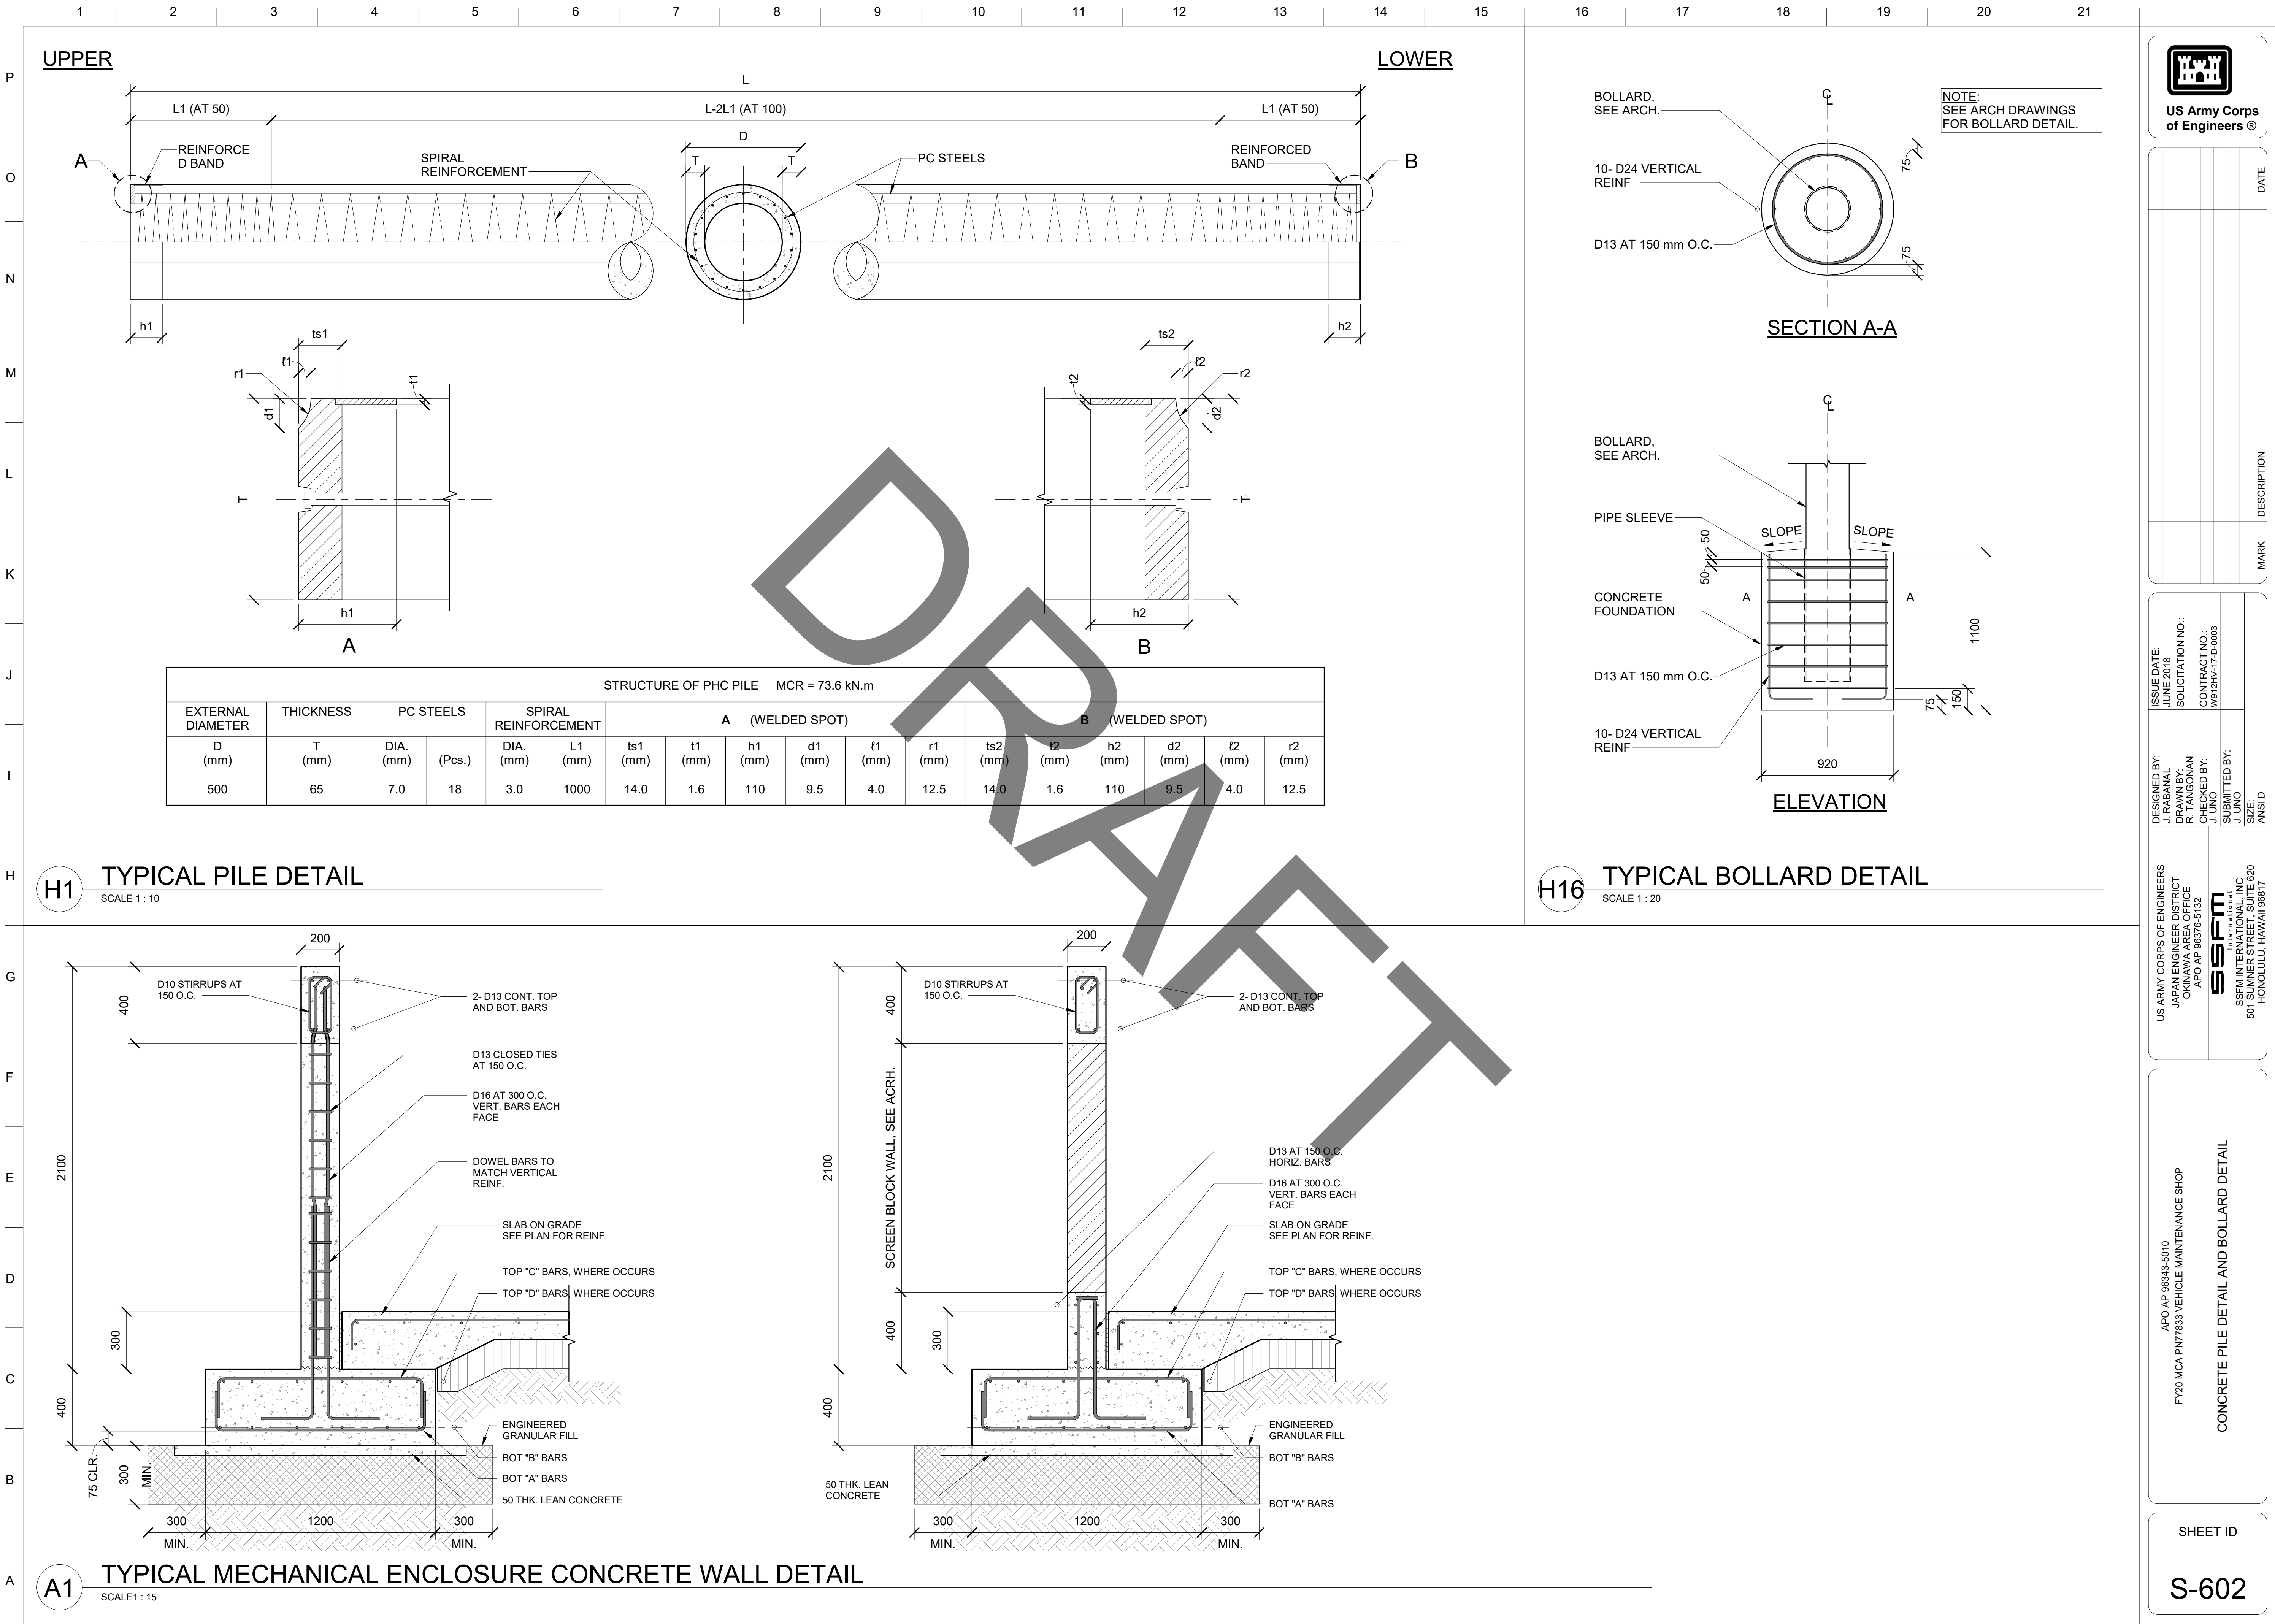

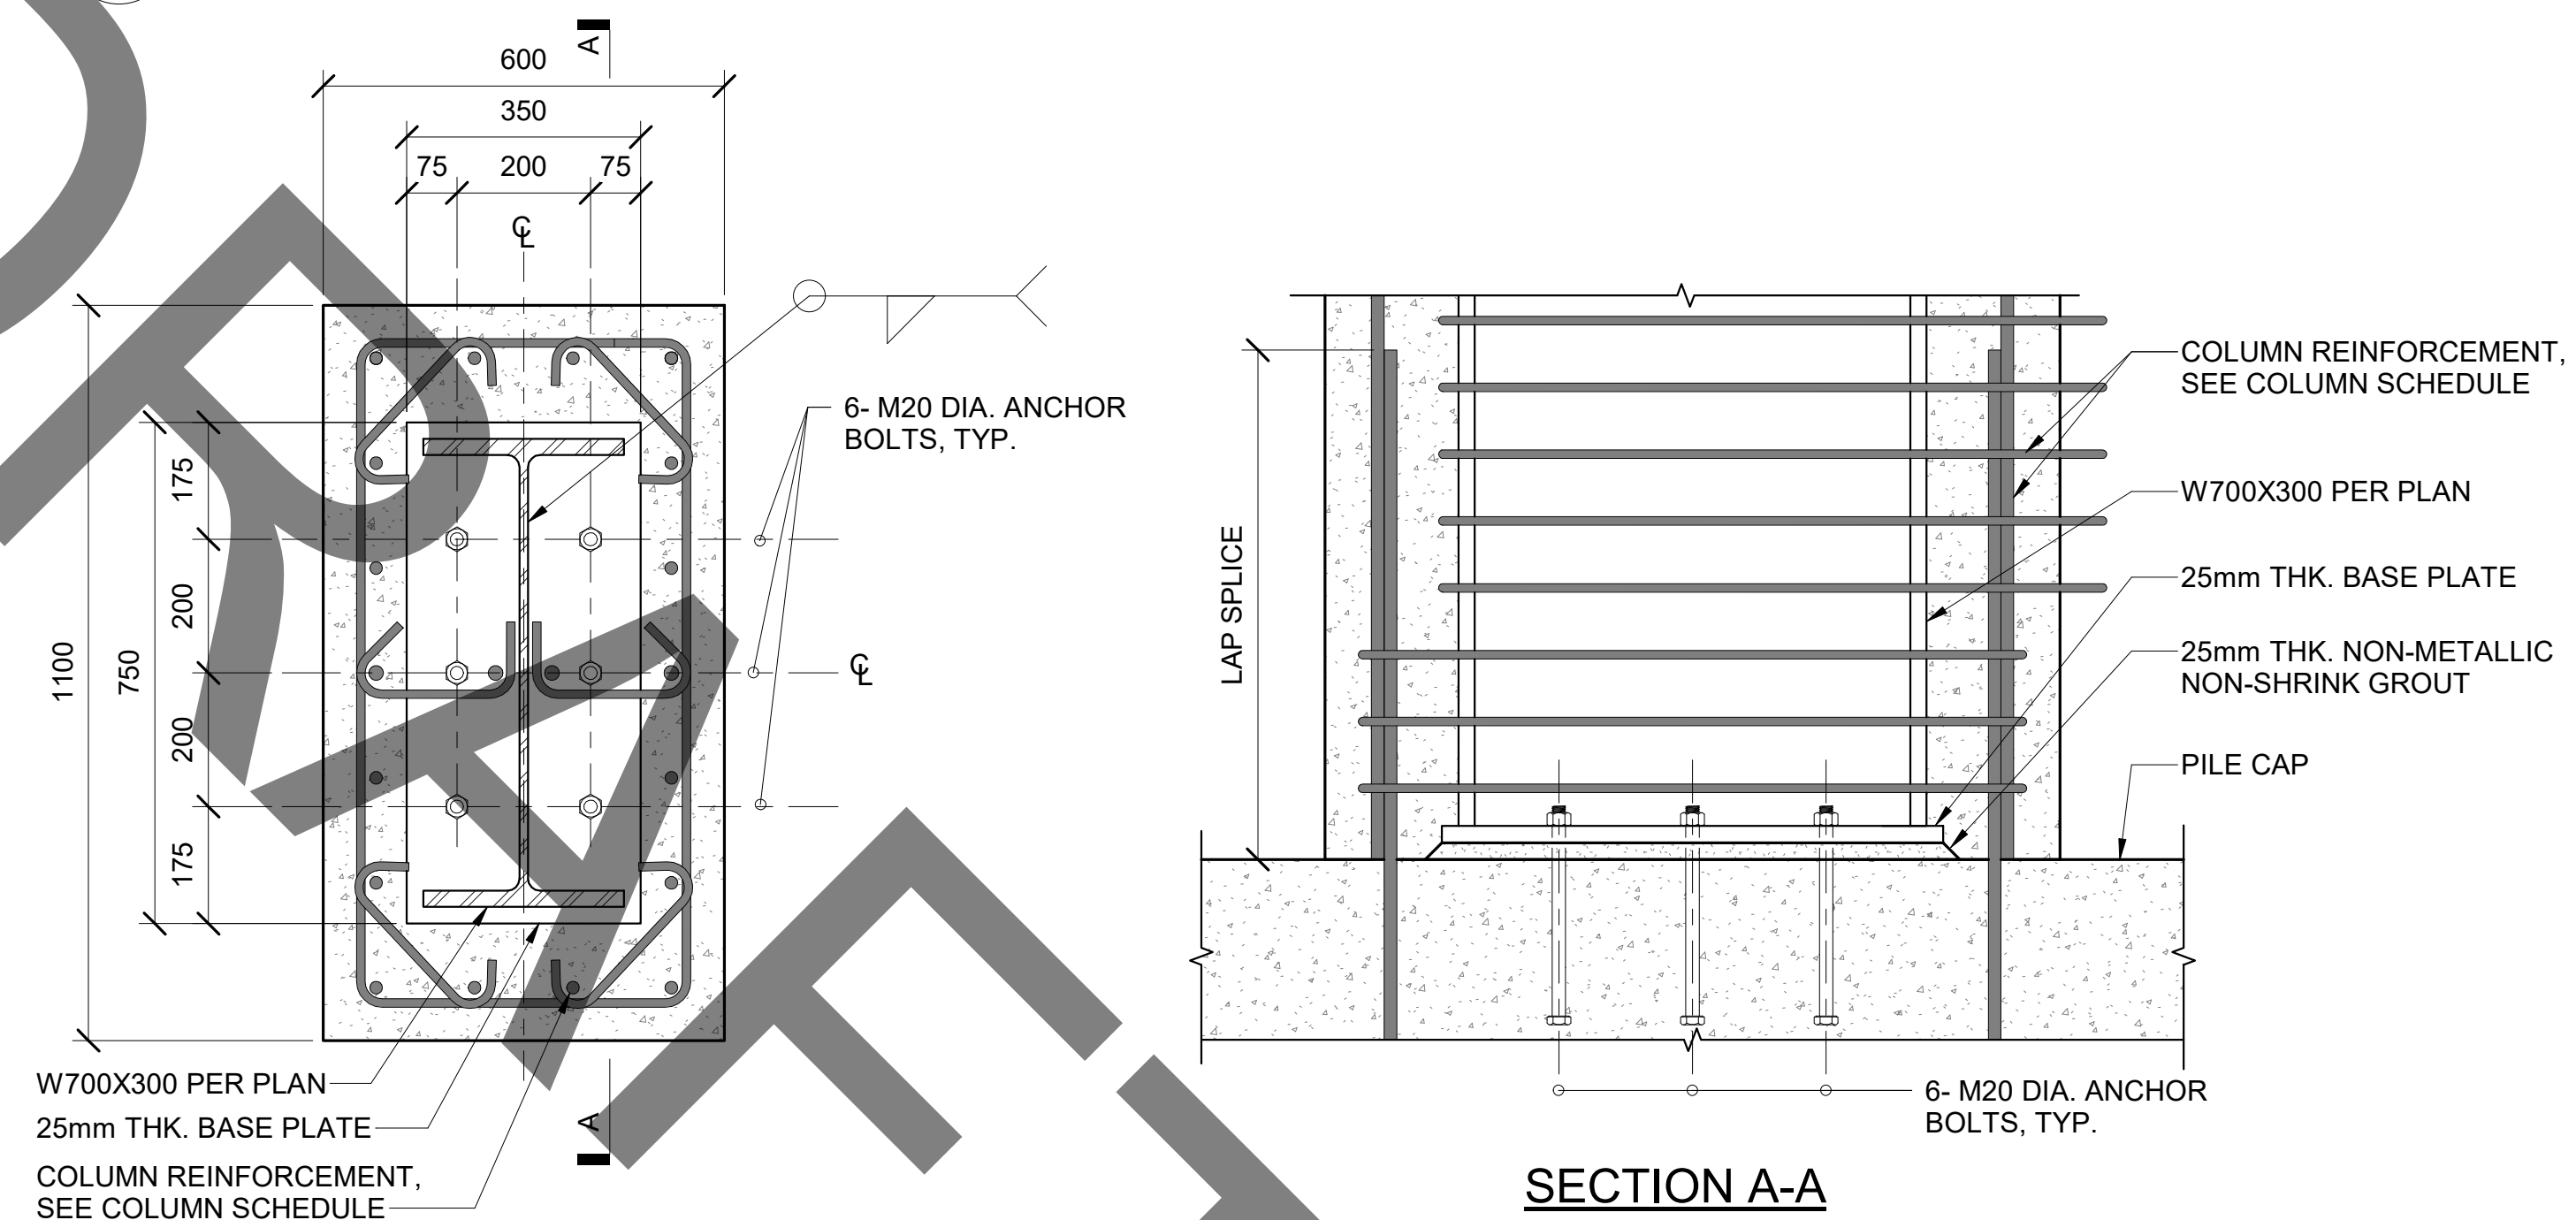

[illegible]

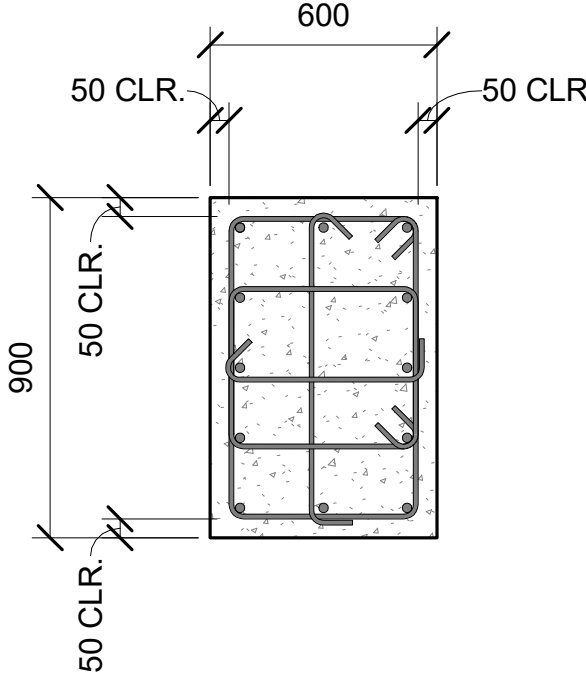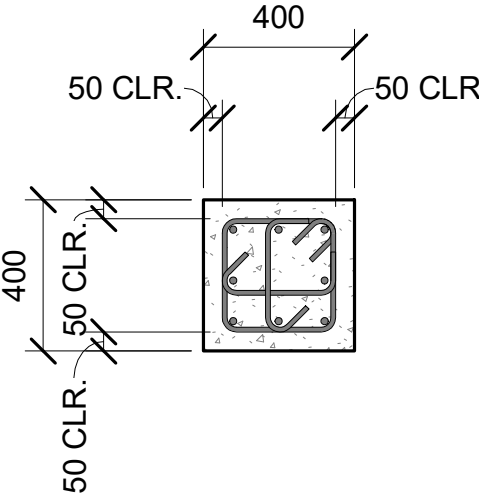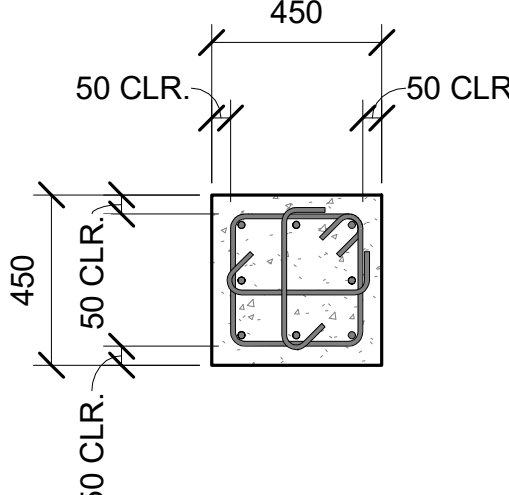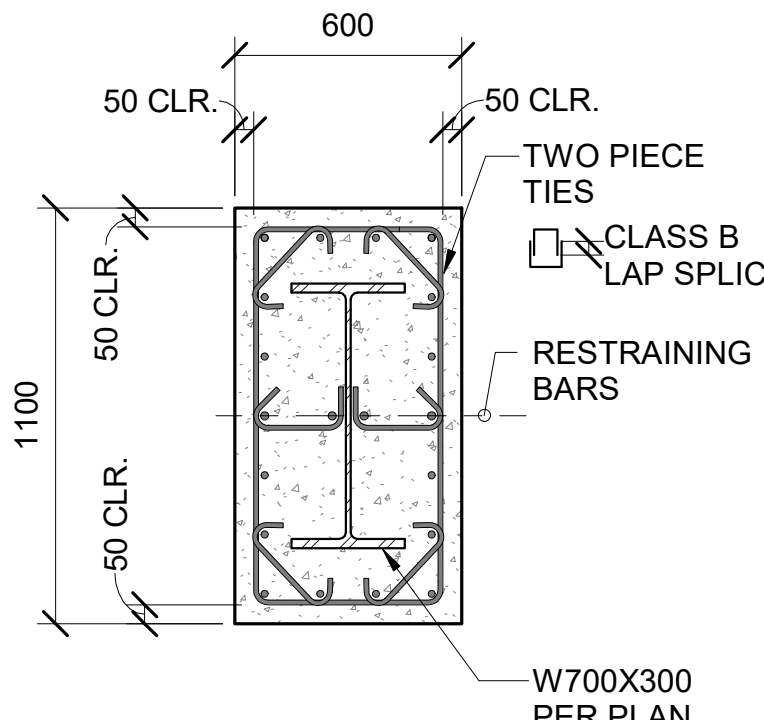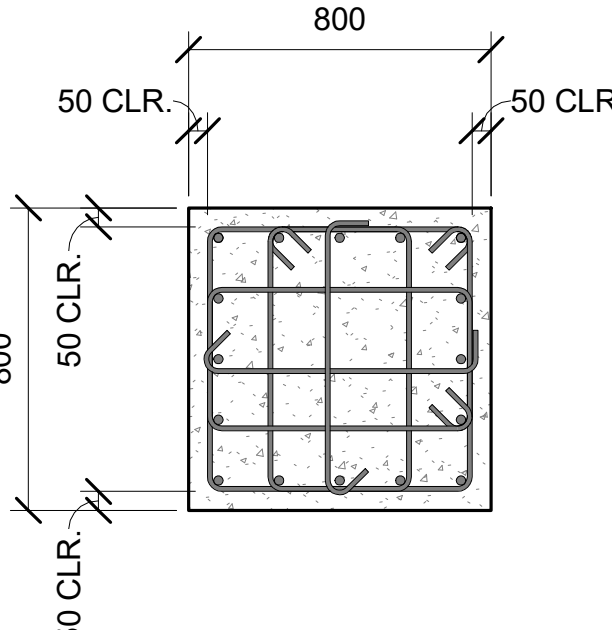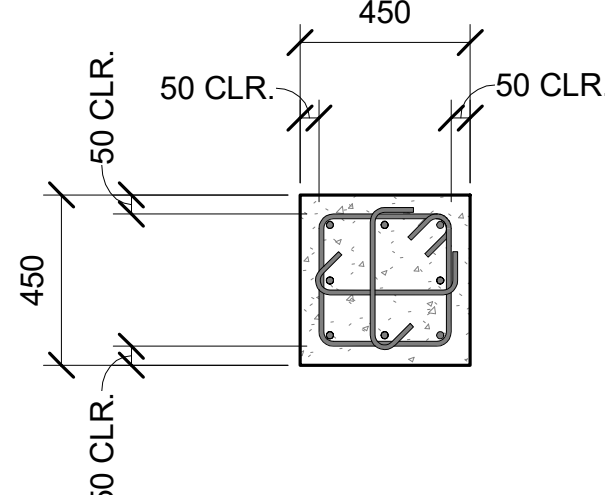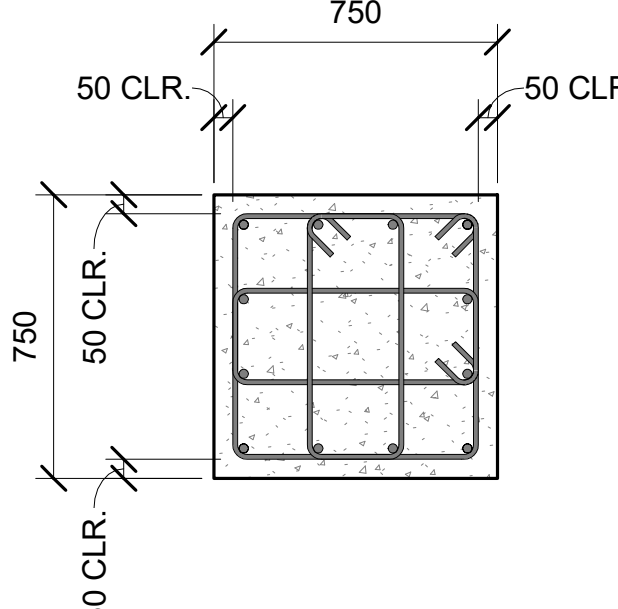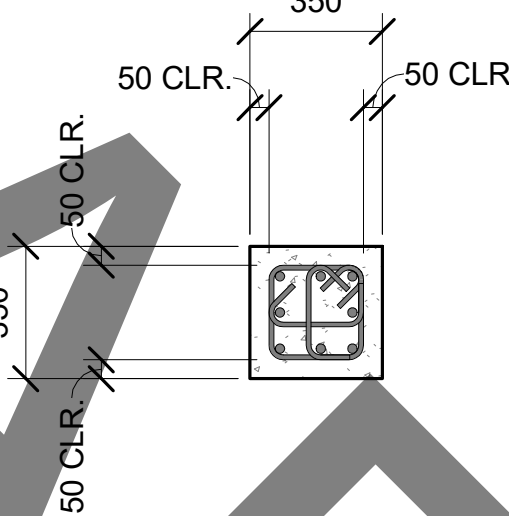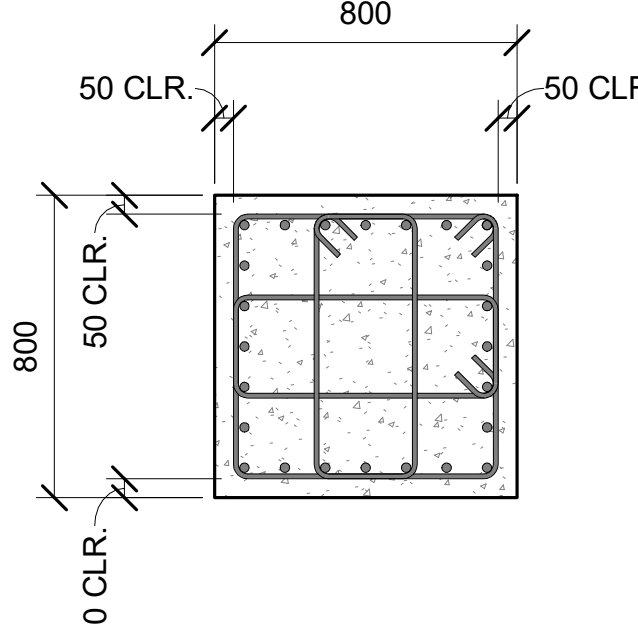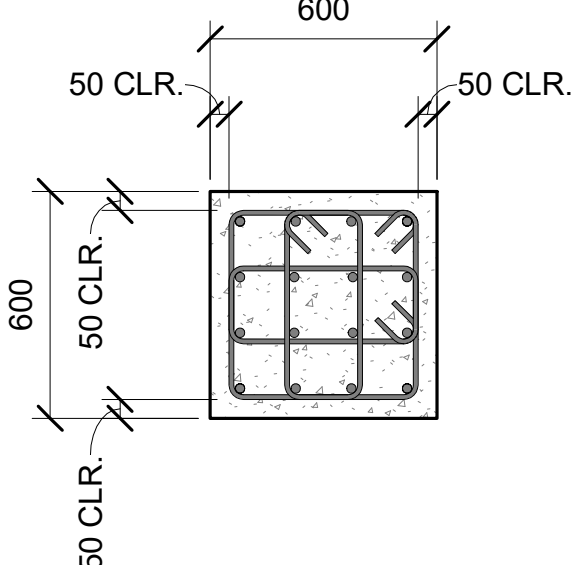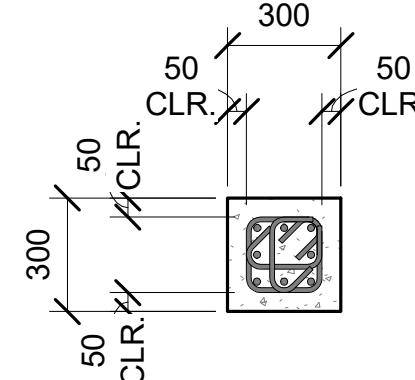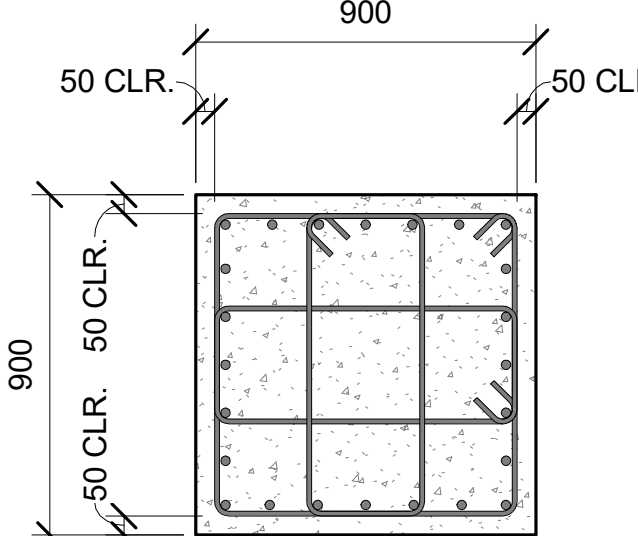CONCRETE COLUMN SCHEDULE																									
FOUNDATION TO ROOF	VEHICLE MAINTENANCE SHOP				ORGANIZATIONAL STORAGE				POL/HAZMAT STORAGE				SSA WAREHOUSE				STORAGE SHED				FIRE PUMP BUILDING				
	C-1A				C-1B				C-1C				C-1D				C-1E				C-1F				
													NOTE: LONGITUDINAL RESTRAINING BARS DISCONTINUES AT BASE OF COLUMN 												
	VERT. BARS:	12- D25			VERT. BARS:	8- D19			VERT. BARS:	8- D19			VERT. BARS:	16- D19	RESTRAINING BARS:	4- D22		VERT. BARS:	16- D25		VERT. BARS:	8- D19			
	TIES:	2 SETS OF CLOSED TIES AND 2 SETS OF CROSS TIES, D13 AT 100mm, BALANCE AT 150mm O.C.			TIES:	1 SET OF CLOSED TIE AND 2 SETS OF CROSS TIES, D13 AT 100mm, BALANCE AT 150mm O.C.			TIES:	1 SET OF CLOSED TIE AND 2 SETS OF CROSS TIES, D13 AT 100mm, BALANCE AT 150mm O.C.			TIES:	1 SET LAPPED TIES, 6 SETS CROSS TIES 1- D13 AT 50mm, 24 AT 100mm, BALANCE AT 150mm O.C.			TIES:	3 SETS OF CLOSE TIE AND 2 SETS OF CROSS TIE, 1- D13 AT 50mm, 13 AT 100mm, BALANCE AT 150mm O.C.		TIES:	1 SETS OF CLOSE TIE AND 2 SETS OF CROSS TIE, D13 AT 100mm, BALANCE AT 150mm O.C.				
	TYPE:	TYPE 1			TYPE:	TYPE 1			TYPE:	TYPE 1			TYPE:	TYPE 1			TYPE:	SMF, TYPE 2		TYPE:	TYPE 1				
	C-2A												C-2D				C-2E								
																									
	VERT. BARS:	12- D25											VERT. BARS:	8- D19			VERT. BARS:	24- D25							
	TIES:	3 SETS OF CLOSED TIES, D13 AT 100mm, BALANCE AT 150mm O.C.											TIES:	1 SET CLOSED TIES, 2 SETS CROSS TIES 1- D13 AT 50mm, 24 AT 100mm, BALANCE AT 150mm O.C.			TIES:	3 SETS OF CLOSE TIE, 1- D16 AT 50mm, 13 AT 100mm, BALANCE AT 150mm O.C.							
	TYPE:	TYPE 1											TYPE:	TYPE 1			TYPE:	SMF, TYPE 2							
	C-3A												C-3D				C-3E								
																									
	VERT. BARS:	16- D25											VERT. BARS:	8- D19			VERT. BARS:	24- D25							
	TIES:	3 SETS OF CLOSE TIE, D13 AT 100mm, BALANCE AT 150mm O.C.											TIES:	1 SET CLOSED TIES, 2 SETS CROSS TIES, 1- D13 AT 50mm, 18 AT 100mm, BALANCE AT 150mm O.C.			TIES:	3 SETS OF CLOSE TIE, 1- D16 AT 50mm, 13 AT 100mm, BALANCE AT 150mm O.C.							
	TYPE:	TYPE 1											TYPE:	TYPE 1			TYPE:	SMF, TYPE 2							



US Army Corps
of Engineers®

ISSUE DATE:
JUNE 2018

SOLICITATION NO.:
W912HV-17-D-0003

CONTRACT NO.:
W912HV-17-D-0003

DESIGNED BY:
J. RABANAL

DRAWN BY:
R. TANGONAN

CHECKED BY:
J. UNO

SUBMITTED BY:
J. UNO

SIZE:
A1SD

US ARMY CORPS OF ENGINEERS
JAPAN ENGINEER DISTRICT
OKINAWA AREA OFFICE
APO AF 96346-5132




SSFM INTERNATIONAL, INC.
507 SUMNER STREET, SUITE 620
HONOLULU, HAWAII 96817

APO AF 96346-5010
FY20 MCA PN7833 VEHICLE MAINTENANCE SHOP

CONCRETE COLUMN SCHEDULE

SHEET ID

S-607

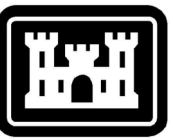

US Army Corps
of Engineers ®

ISSUE DATE:
JUNE 2018

DESIGNED BY:
J. RABANAL

DRAWN BY:
R. TANGONAN

CHECKED BY:
J. UNO

SIZE:
ANSI D

SOLICITATION NO.:
W912RY-17-D-0003

CONTRACT NO.:
W912RY-17-D-0003

SUBMITTED BY:
J. UNO

ISSUED BY:
J. UNO

US ARMY CORPS OF ENGINEERS
JAPAN ENGINEER DISTRICT
OKINAWA AREA OFFICE
APO AP 96376-5132



SSFM
SUNSHINE
FACILITIES
507 SUMNER STREET, SUITE 620
HONOLULU, HAWAII 96817

APO AP 96343-5010
FY20 MCA PN7833 VEHICLE MAINTENANCE SHOP

CONCRETE COLUMN SCHEDULE

SHEET ID

S-607

Plot Date: 12/16/2025 3:42:06 PM

File Path: Autocad Docs \Vehicle Maint Shop\Kadena\511756_TEMPL STRUCT.rvt

INTERMEDIATE DESIGN

US Army Corps of Engineers®

US ARMY CORPS OF ENGINEERS
JAPAN ENGINEER DISTRICT
OKINAWA AREA OFFICE
APO AF 96349-5010

SSFM

INTERNATIONAL, INC

505 KALANANUOULI DRIVE
HONOLULU, HAWAII 96817

DESIGNED BY:
J. RABANAL

DRAWN BY:
R. TANGONAN

CHECKED BY:
J. UNO

SUBMITTED BY:
J

<



**US Army Corps
of Engineers ®**

[illegible]

US ARMY CORPS OF ENGINEERS JAPAN ENGINEER DISTRICT KINAWA AREA OFFICE APO AP 96376-5132	 SSM INTERNATIONAL, INC 500 KALANIANAʻOHE BLVD HONOLULU, HAWAII 96817	DESIGNED BY: J. RABANAL DRAWN BY: J. RABANAL CHECKED BY: J. UNO SUBMITTED BY: J. UNO	ISSUE DATE: JANUARY 2018 SOLICITATION NO.: CONTRACT NO.: W812HV-17-D-0003
--	---	---	---

CONCRETE BEAM SCHEDULE

SHEET ID

S-609

Autodesk Docs: //Vehicle Maint Shop Kadena/511758_TMF_STRUC.nvt


File Path:

Plot Date: 12/16/2025 3:42:13 PM

INTERMEDIATE DESIGN

RETAINING WALL PLAN WITH FENCE

RETAINING WALL FENCE POST DETAILS

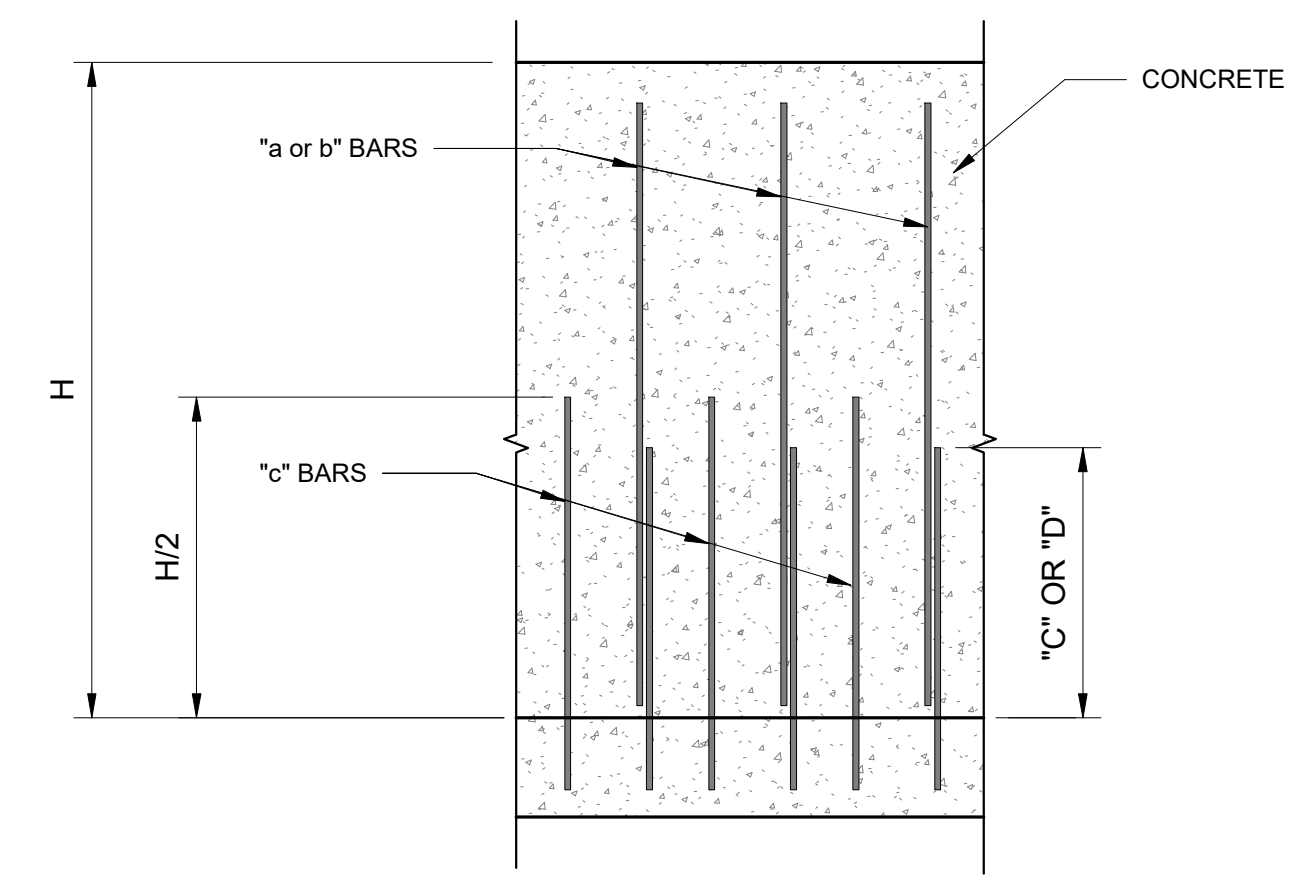

RETAINING WALL ELEVATION

RETAINING WALL SCHEDULE							
WALL MARK	RW-1	RW-2	RW-3	RW-4	RW-5	RW-6	RW-7
H (MAXIMUM)	1000	2000	3000	4000	5000	6000	7000
L	1500	2400	4000	5600	8400	12700	14800
T	600	600	800	900	900	1200	1200
A	-	-	-	1000	1000	2000	2000
B	1500	2400	4000	4600	7400	10700	12800
E	-	-	-	-	-	1000	1000
W	250	300	300	450	800	1200	1600
"a" BARS	D16 AT 300	D16 AT 300	D22 AT 300	D25 AT 300	D25 AT 300	D29 AT 300	D29 AT 300
"b" BARS	D16 AT 300	D16 AT 300	D16 AT 300	D16 AT 300	D16 AT 300	D16 AT 300	D16 AT 300
"c" BARS	D16 AT 300	D16 AT 300	D22 AT 300	D25 AT 300	D25 AT 300	D29 AT 300	D29 AT 300
"d" BARS	D16 AT 300	D16 AT 300	D16 AT 300	D16 AT 300	D22 AT 300	D25 AT 300	D25 AT 300
"f" BARS	D16 AT 300	D16 AT 300	D16 AT 300	D16 AT 300	D16 AT 300	D19 AT 300	D19 AT 300
"g" BARS	D25 AT 300	D25 AT 300	D25 AT 300	D25 AT 250	D25 AT 250	D29 AT 150	D29 AT 150
"h" BARS	D25 AT 300	D25 AT 300	D25 AT 300	D25 AT 250	D25 AT 250	D29 AT 300	D29 AT 300
"j" BARS	-	-	-	-	-	D29 AT 300	D29 AT 300

RETAINING WALL DESIGN CRITERIA

ALLOWABLE SOIL BEARING PRESSURE = 120 kPa

STATIC ACTIVE PRESSURE = 6 kPa/m

STATIC PASSIVE PRESSURE = 65 kPa/m

SEISMIC ACTIVE PRESSURE = 6.72 kPa/m

SEISMIC PASSIVE PRESSURE = 13.03 kPa/m

COEFFICIENT OF FRICTION = 0.45

SURCHARGE = 36 kPa/m

NOTE:

ALL DIMENSIONS SHOWN IN
CALLOUTS/NOTES ARE IN MILLIMETER
UNLESS OTHERWISE NOTED.



**S Army Corps
f Engineers ®**

[illegible]

U.S. ARMY CORPS OF ENGINEERS JANUARY 1967 OKINAWA AREA OFFICE APO AF 96376-5132		JUNE 2018 J. RABANAL DRAWN BY CHECKED BY J. UNO CONTRACT NO.: W912HV-17-D-0003 SUBMITTED BY: J. UNO ANSI D	
--	--	---	--

FY20 MCA PN7833 VEHICLE MAINTENANCE SHOP

[illegible]

SHEET ID

S-611

INTERMEDIATE DESIGN

Plot Date: 12/16/2025 3:42:22 PM File Path:

Autodesk Docs://Vehicle Maint Shop Kadena/511758_TEMF_STRUC.rvt

	1	2	3	4	5	6	7	8	9	10	11	12	13	14	15	16	17	18	19	20	21
	#	POUND OR NUMBER	BOT	BOTTOM		DISP	DISPENSER		GDR	GUARDRAIL	MEZZ	MEZZANINE		PS CONC	PRESTRESSED CONCRETE	SJI	STEEL JOIST INSTITUTE	W/	WITH		
	%	PERCENT	BP	BUILDING PAPER		DIST	DISTANCE		GF/CI	GOVERNMENT FURNISHED CONTRACTOR INSTALLED	MFD	MANUFACTURED		PT	PAINT	SK	SKETCH	W/O	WITHOUT		
P	&	AND	BR	BEDROOM		DMPF	DAMP PROOFING				MFG	MANUFACTURING		PT CONC	POST-TENSIONED CONCRETE	SLD WDW	HORIZONTAL SLIDING WINDOW	WARR	WARRANTY		
	(E)	EXISTING	BS	BOTH SIDES		DOC	DOCUMENT		GFRP	GLASS-FIBER-REINFORCED PLASTIC	MFR	MANUFACTURER		PTD	PAPER TOWEL DISPENSER			WB	WOOD BASE		
	(N)	NEW	BSMT	BASEMENT		DPTN	DEMOUNTABLE PARTITION				MFR REC	MANUFACTURER'S RECOMMENDATION		PTDR	PAPER TOWEL DISPENSER AND RECEPTACLE	SLDG	SLIDING	WBL	WOOD BLOCKING		
	@	AT	BTWN	BETWEEN		DR	DOOR		GL	GLASS						SLNT	SEALANT	WC	WATER CLOSET		
	A/C	AIR CONDITION	C TO C	CENTER TO CENTER		DR CL	DOOR CLOSER		GL BLK	GLASS BLOCK	MIN	MINIMUM		PTN	PARTITION	SM	SHEET METAL	WC WL	WATER CLOSET WALL HUNG		
O	A/E	ARCHITECT / ENGINEER	C&P	CARPET AND PAD		DR FR	DOOR FRAME		GLU LAM	GLUE LAMINATED WOOD	MIRR	MIRROR		PTR	PAPER TOWEL RECEPTACLE	SND	SANITARY NAPKIN DISPENSER	HNG			
	AB	ANCHOR BOLT	CAB	CABINET		DRH	DOOR HOLDER		GOVT	GOVERNMENT	I MJ	MECHANICAL JOINT		PV	PHOTOVOLTAI C			WCL WL	WATER COOLER, WALL MOUNTED		
	ABA	ACCESSIBLE	CATV	COMMUNITY ANTENNA TELEVISION		DRLV	DOOR LOUVER		GR	GROSS	ML	METAL LATH		PVC	POLYVINYL CHLORIDE (PLASTIC)	SNDU	SANITARY NAPKIN DISPOSAL UNIT	WCLR	WATER COOLER		
	ACI	AMERICAN CONCRETE INSTITUTE	CB	CORNER BEAD		DRST	DOOR STOP		GR FL	GROUND FLOOR	MLDG	MOLDING (MOULDING)						WCO	WALL CLEANOUT		
						DRSW	DOOR SWITCH		GRAN	GRANITE	MLWK	MILWORK		PWR	POWER	SNSR	SENSOR	WD	WOOD		
	ACOUS	ACOUSTICAL	CCD	CONTRACT CHANGE DIRECTIVE		DS	DOWN SPOUT		GSB	GYP SUM SHEATHING BOARD	MOD BIT	MODIFIED BITUMEN		QA	QUALITY ASSURANCE	SPCL	SPECIAL	WDF	WOOD DOOR AND FRAME		
N	ACS DR	ACCESS DOOR				DSGN	DESIGN		GSM	GALVANIZED SHEET METAL	MOPR	MOP RACK		QC	QUALITY CONTROL	SPEC	SPECIFICATION	WDMA	WINDOW AND DOOR MANUFACTURERS ASSOCIATION		
	ACS FLR	ACCESS FLOOR	CCTV	CLOSED CIRCUIT TELEVISION		DSPL	DISPOSAL		GUT	GUTTER	MR	MOISTURE RESISTANT		QM	QUALITY MANAGEMENT	SPKLR	SPRINKLER				
	ACS PNL	ACCESS PANEL	CD	CONSTRUCTION DOCUMENTS		DUPL	DUPLICATE		GYM	GYMNASIUM	MRT	MARBLE THRESHOLD		QT	QUARRY TILE	SPLY	SUPPLY				
	ACST	ACOUSTIC	CEM	CEMENT		DW	DISHWASHER		GYP	GYP SUM	MS	MOP SINK		QTY	QUANTITY	SQ	SQUARE				
	ACT	ACOUSTICAL CEILING TILE	CER	CERAMIC		DWG	DRAWING		GYP BD	GYP SUM BOARD	MT	METAL TRESHOLD		R	RADIUS	SS	STANDING SEAM (ROOF)	WDSP	WASTE DISPOSER		
	ADA	AMERICANS WITH DISABILITIES ACT	CERT	CERFTIFY		DWH	DOMESTIC WATER HEATER		H	HIGH	MTD	MOUNTED		RB	RESILIENT BASE	SSP	SOLID SURFACE POLYMER	WDW	WINDOW		
M	ADC	AUTOMATIC DOOR CLOSER	CF	CONTRACTOR FURNISHED		DWR	DRAWER		H PLAM	HIGH PRESSURE PLASTIC LAMINATE	MTG	MOUNTING		RB HK	ROBE HOOK	SST	STAINLESS STEEL	WFR	WOOD FRAME		
	ADDL	ADDITIONAL	CF/CI	CONTRACTOR FURNISHED/CONTRACTOR INSTALLED		DWV	DRAIN, WASTE AND VENT		HAZ	HAZARD	MTL	METAL		RBR	RUBBER	ST	STAIRS	WGL	WIRED GLASS		
	ADDM	ADDENDUM				E	EAST		HAZ MAT	HAZARDOUS MATERIALS	MTLF	METAL FLASHING		RC	REINFORCED CONCRETE	STAG	STAGGERED	WH	WATER HEATER		
	ADJ	ADJACENT	CFE	CONTRACTOR FURNISHED EQUIPMENT		EA	EACH		HB	HOSE BIBB	MTLR	METAL ROOF		RCP	REFLECTED CEILING PLAN	STC	SOUND TRANSMISSION CLASS	WHSE	WAREHOUSE		
	ADMIN	ADMINISTRATION				EE	EACH END		MULL	MULLION	N	NORTH		RCPTN	RECEPTION			WM	WATER METER		
	ADS	AUTOMATIC DOOR SEAL	CFMF	COLD-FORMED METAL FRAMING		EF	EACH FACE		HC	HOLLOW CORE	N			RD	ROOF DRAIN	STD	STANDARD	WO	WHERE OCCURS		
L	AFF	ABOVE FINISH FLOOR	CG	CORNER GUARD		EFS	EXTERIOR FINISH SYSTEM		HCWD	HOLLOW CORE WOOD DOOR	NA	NOT APPLICABLE		RDG INS	RIDGID INSULATION, SOLID	STL JST	STEEL JOIST	WP	WEATHERPROOF		
	AFG	ABOVE FINISH GRADE	CH	COAT HOOK		EGB	EXTERIOR GYP SUM BOARD		HD	HAND DRYER	NE	NOT EXCEEDING		REBAR	REINFORCING STEEL BARS	STOR	STORAGE	WPM	WATERPROOF MEMBRANE		
	AFS	ABOVE FINISH SLAB	CH	CHALKBOARD		EHD	ELECTRIC HAND DRYER		HDPE	HIGH DENSITY POLYETHYLENE	NEC	NATIONAL ELECTRIC CODE		REC	RECESSED	STRUCT	STRUCTURAL	WR	WEATHER RESISTANT		
	AHJ	AUTHORITY HAVING JURISDICTION	CH BD			ELAST	ELASTOMERIC		HDR	HEADER	NFRC	NATIONAL FENESTRATION RATING COUNCIL		REC ROOM	RECREATION ROOM	SUB	SUBSTITUTE	WS	WEATHERSTRIP		
			CHFR	CHAMFER		ELEV	ELEVATOR		HM	HOLLOW METAL						SUPPL	SUPPLEMENT	WSCT	WAINSCOT		
K	AHR	ANCHOR	CI	CAST IRON		EM	EMERGENCY		HMD	HOLLOW METAL DOOR	NIC	NOT IN CONTRACT		RECD	RECEIVED	SURF	SURFACE	WSL	WEATHER SEAL		
	AIA	AMERICAN INSTITUTE OF ARCHITECTS	CIP	CAST-IN-PLACE		ENCL	ENCLOSURE		HMDF	HOLLOW METAL DOOR AND FRAME	NO	NUMBER		RECT	RECEPTACLE	SURR	SURROUND	WU	WINDOW UNIT		
			CJ	CONSTRUCTION JOINT		ENGR	ENGINEER				NRC	NOISE REDUCTION COEFFICIENT		REF	REFRIGERATOR	SURV	SURVEY	WW	WASTE WATER		
	AISC	AMERICAN INSTITUTE OF STEEL CONSTRUCTION	CL	CENTER LINE		EOS	EDGE OF SLAB		HNDRL	HANDRAIL						SUSP	SUSPEND	WWR	WELDED WIRE REINFORCEMENT		
			CLG	CEILING		EPA	ENVIRONMENTAL PROTECTION AGENCY				NRP	NONREMOVEABLE PIN		REINF	REINFORCE	SUSP CLG	SUSPENDED CEILING				
	ALLOW	ALLOWANCE	CLO	CLOSET					HO	HOLD OPEN	NS	NO SCALE		REM	REMOVABLE	SV	SHEET VINYL	X	BY		
J	ALT	ALTERNATE	CLR	CLEAR		EPS	EXPANDED POLYSTYRENE BOARD (INSULATION)		HORIZ	HORIZONTAL	NTP	NOTICE TO PROCEED		REP	REPAIR						
	ALTRN	ALTERATION	CLRM	CLASSROOM		EQ	EQUAL		HS	HAND SINK	O/	OVER		REPL	REPLACE	SVCE	SERVICE	XPS	EXTRUDED POLYSTYRENE BOARD		
	ALUM	ALUMINUM	CM	CONSTRUCTION MANAGEMENT		HSE	HOUSE		HO	HOUSEKEEPING	OA	OVERALL		REQ	REQUIRE	SWDR	SWING DOOR	°	DEGREES		
	AMT	AMOUNT				HSPKG	HOUSEKEEPING		HT	HEIGHT	OF	OUTSIDE FACE		REQD	REQUIRED	SYM	SYMBOL	°	SQUARED		
	ANG	ANGLE	CMU	CONCRETE MASONRY UNIT		EQUIP	EQUIPMENT		OFF	OFFICE	OFF	OFFICE		RESIL	RESILIENT	SYS	SYSTEM	°	SQUARED		
	ANOD	ANODIZE	CNR	CORNER		EQUIV	EQUIVALENT		HVAC	HEATING, VENTILATING, AND AIR CONDITIONING	OF	OUTSIDE FACE OF STUDS		RESL	RESILIENT	T	TREAD	Ø	DIAMETER		
	ANSI	AMERICAN NATIONAL STANDARDS INSTITUTE	CNTR	COUNTER		ERD	EXISTING ROOF DRAIN		OH	OVERHANG	OF	OUTSIDE FACE OF STUDS		REV	REVISION	T&G	TOUNGE AND GROOVE				
			CO	CASED OPENING		ESH	EXHAUST		OPNG	OPENING	OH	OVERHANG		RF	RESILIENT FLOORING	T/S	TUB/SHOWER				
	APC	ACOUSTICAL PANEL CEILING	COL	COLUMN		ESMT	EASEMENT		OPP	OPPOSITE	OPNG	OPENING		RF	RESILIENT FLOORING	TB	TOWEL BAR				
	APPD	APPROVED	COMB	COMBINATION, COMBINED		ETC	ET CETERA		OPQ	OPAQUE	OPP	OPPOSITE		RF	RESILIENT FLOORING	TC	TERRA COTTA				
	APPROX	APPROXIMATE	COMM	COMMUNICATION		EW	ELECTRIC WATER HEATER		OPQ	OPAQUE	OPQ	OPAQUE		RFI	REQUEST FOR INFORMATION	TCA	TILE COUNCIL OF AMERICA				
	APPX	APPENDIX	COMPL	COMPLETE		EW	ELECTRIC WATER HEATER		OPR	OPERABLE	OPR	OPERABLE		RFP	REQUEST FOR PROPOSAL	TD	TRENCH DRAIN				
H	ARCH	ARCHITECT, ACRCHITECTURAL	CONC	CONCRETE		EXP	EXPAND		OPT	OPTIONAL	OR	OUTSIDE RADIUS		RH	ROBE HOOK	TEL	TELEPHONE				
			COND	CONDITION		EXST	EXISTING		OR	OUTSIDE RADIUS	OSHA	OCCUPATIONAL SAFETY AND HEALTH ADMINISTRATION		RL	ROOF LEADER	TEMP	TEMPORARY				
	ARF	ARCHITECTURAL FINISH	CONF	CONFERENCE		EXST GR	EXISTING GRADE		OVFL	OVERFLOW	RM	ROOM		RO	ROUGH OPENING	TFF	TOP OF FINISH FLOR				
	ASHRAE	AMERICAN SOCIETY OF HEATING, REFRIGERATING, AND AIR CONDITIONING ENGINEERS	CONF	CONFERENCE		EXT	EXTERIOR		INCL	INCLUDED	RO	ROUGH OPENING		RR	RESTROOM	THK	THICKNESS				
			CONSTR	CONSTRUCTION		FAS	FASCIA		INSTL	INSTALL	RR	RESTROOM		RST	REINFORCING STEEL	THRESH	THRESHOLD				
			CONT	CONTINUE, CONTINUOUS		FC	FILE CABINET		INSUL	INSULATION	PA	PUBLIC ADDRESS		RT	RIGHT	THRU	THROUGH				
G			COORD	COORDINATE		FD	FLOOR DRAIN		INSUL	INSULATED METAL PANEL	PAR	PARAPET		RTF	RUBBER TILE FLOORING	TMPD	TEMPERED				
	ASI	ARCHITECT'S SUPPLEMENTAL INSTRUCTION	COR	CHANGE ORDER REQUEST		FDC	FIRE DEPARTMENT CONNECTION		PAT	PATTERN	PART	PARTIAL		RTG	RATING	TMPD GL	TEMPERED GLASS				
			CPT	CARPET		INT	INTERIOR		PB	PAINTED BASE	PAT	PATTERN		RVL	REVEAL	TN	TRUE NORTH				
	ASME	AMERICAN SOCIETY OF MECHANICAL ENGINEERS	CR	CLOSET ROD		IS	INSECT SCREEN		PED	PEDISTAL	PB	PAINTED BASE		S	SOUTH	TO	TOP OF				
			CRT YD	COURTYARD		ISO	INTERNATIONAL STANDARDS ORGANIZATION		PCC	PRECAST CONCRETE	PEND	PENDANT		S	SOUTH	TOC	TABLE OF CONTENT				
	ASR	AUTOMATIC SPRINKLER RISER	CSB	CONCRETE SPLASH BLOCK		FEC	FIRE EXTINGUISHER CABINET		PCT	PERCENT	PCT	PERCENT		SALV	SALVAGE	TOL	TOLERANCE				
F			CSG	CASING		FF&E	FURNITURE, FIXTURE, AND EQUIPMENT		PED	PEDISTAL	PERF	PERFORATED		SAT	SUSPENDED ACOUSTICAL TILE	TPD	TOILET PAPER DISPENSER				
	ASSN	ASSOCIATION	CSI	CONSTRUCTION SPECIFICATIONS INSTITUTE		JS	JANITOR'S SINK		PEJ	PREMOLDED EXPANSION JOINT	PERF	PERFORATED		SATC	SUSPENDED ACOUSTICAL TILE CEILING	TPH	TOILET PAPER HOLDER				
	ASSY	ASSEMBLY	FG	FINISH/FINISHED GRADE		KB	KNEE BRACE				PERM	PERIMETER				TRTD	TREATED				
	ASTM	AMERICAN SOCIETY FOR TESTING AND MATERIALS	FGL	FIBERGLASS		KIT	KITCHEN		PEND	PENDANT	PERM	PERIMETER		SB	SPLASH BLOCK	TYP	TYPICAL				
			CSMT	CASEMENT		KPL	KICKPLATE		PERF	PERFORATED	PERP	PERPENDICULAR		SBSTR	SUBSTRATE	UC	UNDERCUT				
	ASWG	AMERICAN STEEL WIRE GAUGE	CSWK	CASEWORK		L	ANGLE		PERM	PERIMETER	PERP	PERPENDICULAR		SC	SOLID CORE	UCD	UNDERCUT DOOR				
E			CT	CERAMIC TILE		L CL	LINEN CLOSET		PERP	PERPENDICULAR	PH	PENTHOUSE		SCD	SEAT COVER DISPENSER	UL	UNDERWRITERS LABORATORIES				
	ATCH	ATTACH, ATTACHMENT	CTB	CERAMIC TILE BASE		FHP	FULL HEIGHT PARTITION		PH	PENTHOUSE	PK LOT	PARKING LOT		SCHD	SCHEDULE	UN	UNLESS NOTED				
	ATTN	ATTENTION	CTF	CERAMIC TILE FLOOR		FIN	FINISH		PK LOT	PARKING LOT	PKG	PACKAGE		SCP	SCUPPER	UNO	UNLESS NOTED OTHERWISE				
	AWI	AMERICAN WOODWORKING INSTITUTE	CTI	CERAMIC TILE INSTITUTE OF AMERICA		FIN FLR	FINISH FLOOR		PKG	PACKAGE	PL	PROPERTY LINE		SCR	SHOWER CURTAIN ROD	UPS	UNINTERRUPTIBLE POWER SUPPLY				
			CTR	COUNTER		FIN GR	FINISH GRADE		PLB	PLUMB	PL	PROPERTY LINE		SCR	SHOWER CURTAIN ROD	UPS	UNINTERRUPTIBLE POWER SUPPLY				
	AWT	ACOUSTICAL WALL TREATMENT	CW	CASEMENT WINDOW		FIXT	FIXTURE		PLB	PLUMB	PLB	PLUMB		SCRN	SCREEN	UR	URINAL				
D			d	DEEP, DEPTH		FLASH	FLASHING		PLBG	PLUMBING	PLYWD	PLYWOOD		SCWD	SOLID CORE WOOD DOOR	UTIL	UTILITY				
	BALC	BALCONY	d	PENNY (NAIL SIZE)		FLR	FLOOR		PLYWD	PLYWOOD	LC	LAUNDRY CHUTE		SD	SOAP DISPENSER	VAN	VANITY				
	BAT	BATTEN	D-B	DESIGN-BUILD		FM	FACTORY MUTUAL		PMTL	PAINTED METAL	LDG	LANDING		SDG	SIDING	VAR	VARIES				
	BB	BASEBOARD	DBL	DOUBLE		FN	FENCE		PNL	PANEL	LDR	LEADER		SDI	STEEL DOOR INSTITUTE	VB	VINYL BASE				
	BC	BOTTOM CORD	DBL	DOUBLE		FOS	FACE OF STUD		POLY	POLYETHYLENE (PLASTIC)	LKR	LOCKER		SECT	SECTION	VCT	VINYL COMPOSITION TILE				
	BD	BOARD	DEF	DEFINITION		FP	FIRE PROTECTION		PORC	PORCELAIN	LNDS	LANDSCAPE		SEL	SELECT	VERT	VERTICAL				
C	BDRY	BOUNDARY	DEG	DEGREE		FR	FIRE RATING		PORT	PORTAL	LR	LIVING ROOM		SEP	SEPARATE	VEST	VESTIBULE				
	BHMA	BUILDER'S HARDWARE MANUFACTURER'S ASSOCIATION	DEL	DELETE		FRA	FIRE RATED ASSEMBLY		PP	PUSH/PULL	LVD	LOUVERED		SF	SQUARE FOOT (FEET)	VFAT	VINYL FACED ACOUSTICAL TILE				
			DEMO	DEMOLITION, DEMOLISH		FRMG	FRAMING		PR	PAIR	LVDR	LOUVERED DOOR		SGD	SLIDING GLASS DOOR						
			DEPT	DEPARTMENT		LVR	LOUVER		PRCST	PRECAST	LVR	LOUVER		SGL	SINGLE	VIC	VICINITY				
	BI FLD DR	BI FOLDING DOORS	DES	DESIGNATE, DESIGNATION		LWC	LIGHTWEIGHT CONCRETE		PREF	PREFERENCE	MACH RM	MACHINE ROOM		SH	SINGLE HUNG	VIF	VERIFY IN FIELD				
	BKBD	BACKBOARD	DESCR	DESCRIBE, DESCRIPTION		FRZ	FREEZER		PREFAB	PREFABRICATE	MAINT	MAINTENANCE		SHFT	SHAFT (ELEVATOR)	VNR	VENEER				
B	BKG	BACKING	DET	DETAIL		FSP	FIRE STANDPIPE		PREFIN	PREFINISH	FT	FOOT, FEET		SHR	SHOWER	VOC	VOLITILE ORGANIC COMPOUND				
	BLDG	BUILDING	DF	DRINKING FOUNTAIN		FT	FOOT, FEET		PREFMD	PREFORMED	MATL	MATERIAL		SHR HD	SHOWER HEAD						
	BLKT	BLANKET	DH	DOUBLE HUNG		FTG	FOOTING		PRELIM	PRELIMINARY	MAX	MAXIMUM		SHRD	SHOWER DRAIN						
	BLT	BUILT	DHI	DOOR HARDWARE INSTITUTE		FURG	FURRING		PREP	PREPARATION	MBH	MOP/BROOM HOLDER		SHT	SHEET	VOL	VOLUME				
	BLW	BELOW	DHW	DOUBLE HUNG WINDOW		FURN	FURNITURE		PREP	PREPARATION	MD										

	1	2	3	4	5	6	7	8	9	10	11	12	13	14	15	16	17	18	19	20	21							
	GENERAL NOTES									MATERIAL SYMBOLS					GRAPHIC SYMBOLS													
P	1	CONTRACTOR SHALL VERIFY EXISTING CONDITIONS AND DIMENSIONS AT THE JOB SITE AND IMMEDIATELY NOTIFY THE CONTRACTING OFFICER OF ANY DISCREPANCIES BEFORE COMMENCING WITH WORK. COMMENCEMENT OF WORK SIGNIFIES ACCEPTANCE OF EXISTING CONDITIONS.								SAND / MORTAR CONCRETE - CAST IN PLACE OR PRECAST STONE PLYWOOD EARTH COMPACTED FILL ROCK FILL ACOUSTIC TILE OR BOARD INSULATION, BATT INSULATION, RIGID ASPHALT CONCRETE GYPSUM BOARD METAL OMIT INDICATION ON THIN MATERIAL OMIT DOUBLE LINES AT SMALL SCALE GLASS OMIT INDICATION ON THIN MATERIAL CERAMIC TILE SHOW PROFILE ONLY WOOD, FINISH					NUMBER INDICATES BUILDING SECTION X-X SHEET NUMBER WHERE SECTION IS DRAWN BUILDING SECTION/ ELEVATION NUMBER INDICATES BUILDING SECTION X-X SHEET NUMBER WHERE SECTION IS DRAWN DETAIL SECTION NUMBER INDICATES DETAIL XX X-X SHEET NUMBER WHERE DETAIL IS DRAWN DETAIL ENLARGEMENT LOCATION OF ADJACENT DRAWING X/X-XXX MATCH LINE MATCHLINE VIEW TITLE 1:200 DRAWING SCALE A101 SHEET NUMBER DRAWING TITLE PLAN NORTH TRUE NORTH PLAN NORTH NORTH ARROW SCALE: 1 : 100 0 2000 4000 GRAPHIC SCALE DIMENSION CLR DIMENSION CLR DIMENSION DIM DIMENSION DIM DIMENSION DIM STANDARD DIMENSIONING DIMENSION TAKEN FROM FACE OF FRAMING TO FACE OF FRAMING, UNLESS NOTED OTHERWISE. WHERE DRAWINGS INDICATE THE FACE OF FINISH IS THE SAME AS FACE OF FRAMING (I.E. CMU, CONCRETE, EXPOSED STRUCTURAL STEEL, EXPOSED WOOD, ETC.). DIMENSION SHALL BE TAKEN FROM FACE OF FRAMING DIMENSIONS TAKEN FROM FACE OF FRAMING MEMBER (I.E. CMU, STRUCTURAL STEEL, WOOD, ETC.) TO FACE OF FRAMING MEMBER.							ROOM NAME 101 ROOM NUMBER 150 SF AREA (WHERE OCCURS) ROOM TAG ROOM NAME 101 ROOM NUMBER +3000 CEILING HEIGHT REFLECTED CEILING TAG D101 DOOR TAG WINDOW TAG XXX PARTITION TYPE TAG 22 RF1 XXX REVISION TAG NAME ELEVATION BUILDING LEVEL 00 FURNITURE TAG XX BUILDING GRID ? KEYNOTE SIGNAGE TYPE LOCATION 1 - INTERIOR 2 - EXTERIOR SIGNAGE TAG (ARCHITECTURE DWGS ONLY)						
	2	THE CONTRACTOR IS TO FOLLOW DIRECTIONS OF ONLY THE CONTRACTING OFFICER OR THEIR AUTHORIZED REPRESENTATIVE. CONTRACTOR SHALL PROVIDE COPIES OF APPROVED PERMITS TO THE CONTRACTING OFFICER PRIOR TO BEGINNING ANY EXCAVATION WORK.																										
O	3	ALL WORK SHALL STRICTLY CONFORM TO ALL APPLICABLE LOCAL AND FEDERAL CODES, STANDARDS, AND REGULATIONS. EXPOSED CONCRETE FOUNDATIONS (BETWEEN SIDING AND FINISH GRADE) SHALL BE CEMENT WASHED AND PAINTED.																										
	4	THE CONTRACTOR SHALL BE RESPONSIBLE FOR ANY LOSS OR DAMAGE OF EXISTING PROPERTY AND CONDITIONS TO REMAIN, RESULTING FROM CONSTRUCTION ACTIVITIES, AND SHALL MAKE GOOD ANY LOSS, DAMAGE, OR INJURY WITHOUT COST TO THE GOVERNMENT.																										
	5	CONSTRUCTION ACTIVITIES SHALL NOT DISRUPT EXISTING ONGOING OPERATIONS IN THE VICINITY.																										
N	6	CONFINE ALL OPERATIONS TO AREAS SPECIFICALLY AUTHORIZED BY THE GOVERNMENT. KEEP WORK AREAS AND ADJACENT TO THE WORK AREA FREE FROM ACCUMULATION OF TRASH AND DEBRIS.																										
	7	CONTRACTOR TO FIELD VERIFY ALL EQUIPMENT AND MATERIAL SIZES AND PROVIDE ADEQUATE CLEARANCE AS REQUIRED, BEFORE PROCEEDING WITH THE WORK.																										
	8	FOR ANY APPROVED SUBSTITUTIONS, CONTRACTOR IS RESPONSIBLE TO PROVIDE A COMPLETE AND WORKING COMPONENT AND MUST BEAR ALL NEW INCIDENTAL COSTS IMPACTED BY THE APPROVED SUBSTITUTION REQUEST.																										
	9	CONTRACTOR SHALL VERIFY ALL APPLIANCE REQUIREMENTS AND STUB-OUT LOCATIONS.																										
M	10	UPON COMPLETION, REMOVE FOREIGN MATERIALS FROM ALL EXPOSED SURFACES AND CLEAN THOROUGHLY.																										
	11	FOLLOW SPEC SECTION 01 74 19 - "CONSTRUCTION AND DEMOLITION WASTE MANAGEMENT" FOR PROPER DISPOSAL OF CONSTRUCTION AND DEMOLITION DEBRIS. CONTRACTOR SHALL BE RESPONSIBLE FOR REMOVAL AND DISPOSAL OF ALL CONSTRUCTION MATERIAL, UNLESS NOTED OTHERWISE. OP INSTALLER TO CAULK ALL INSIDE CORNERS WHERE COUNTERTOPS / BACKSPLASHES MEET CABINET AND / OR GYPSUM BOARD																										
	12	ALL EXISTING EXTERIOR WINDOWS ARE TO REMAIN AND SHALL BE PROTECTED DURING THE DEMOLITION AND CONSTRUCTION PHASES OF THE PROJECT. ANY DAMAGE TO THE STRUCTURAL INTEGRITY OF THE WINDOW FRAMES, GLAZING AND ACCESSORIES SHALL BE REPLACED AT NO ADDITIONAL COST TO THE GOVERNMENT.																										
L	13	WHERE DEMOLITION AND CUTTING WORK HAS OCCURRED OR WHERE EXISTING SURFACES, MATERIALS OR OTHER ITEMS HAVE BEEN DAMAGED OR DISTURBED AS A RESULT OF THIS CONTRACT, THE SAID SURFACES AND AREAS SHALL BE CAREFULLY CLOSED UP, PATCHED AND FINISHED, AND OR RESTORED AS REQUIRED TO BE CONTIGUOUS TO EXISTING SURROUNDING SURFACES.																										
	14	THE GENERAL CONTRACTOR, AT THE COMPLETION OF THIS WORK, SHALL LEAVE ALL WORK AREAS AND FINISHED SPACES IN A CLEAN AND ACCEPTABLE CONDITION. FINAL CLEAN-UP INCLUDES, BUT NOT LIMITED TO: ALL INTERIOR SURFACES, LIGHT FIXTURES, PLUMBING FIXTURES, APPLIANCES, INTERIOR OF WINDOWS, SILLS ETC.																										
K	15	ALL JOINTS AND PENETRATIONS (MEMBRANE AND THROUGH PENETRATIONS) IN FIRE OR SMOKE RESISTIVE ASSEMBLIES SHALL BE PROPERLY FIRE STOPPED W/ FM MUTUAL OR UL APPROVED MATERIALS, MEANS AND METHODS.																										
J																												
I																												
H																												
G																												
F																												
E																												
D																												
C																												
B																												
A																												

US Army Corps of Engineers®

DATE

DESCRIPTION

MARK

ISSUE DATE:

DESIGNED BY: KELLINGWOOD

DRAWN BY: TROLLO, J. MANUUA

CHECKED BY: D. HICKS

SUBMITTED BY:

SHEET NO.: 0003

CONTRACT NO.: W912TV-17-D-0003

SIZE: ANS I D

US ARMY CORPS OF ENGINEERS

JAPAN ENGINEER DISTRICT

OKINAWA AREA OFFICE

APO AP 96345-5132

DESIGN PARTNERS INCORPORATED

1580 MAKALOA STREET, SUITE 1100

HONOLULU, HAWAII 96814



APO AP 96345-5010


FY20 MCA PN77833 VEHICLE MAINTENANCE SHOP




GENERAL NOTES, SYMBOLS & CLIN SCHEDULE


SHEET ID


A-002

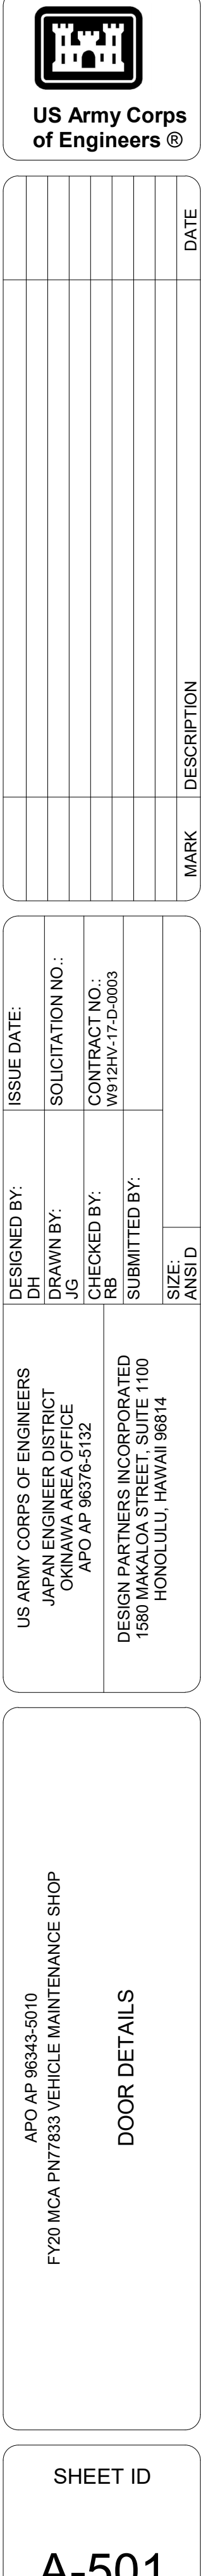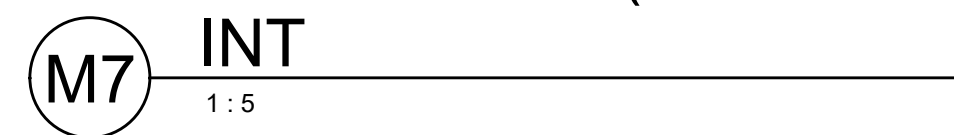

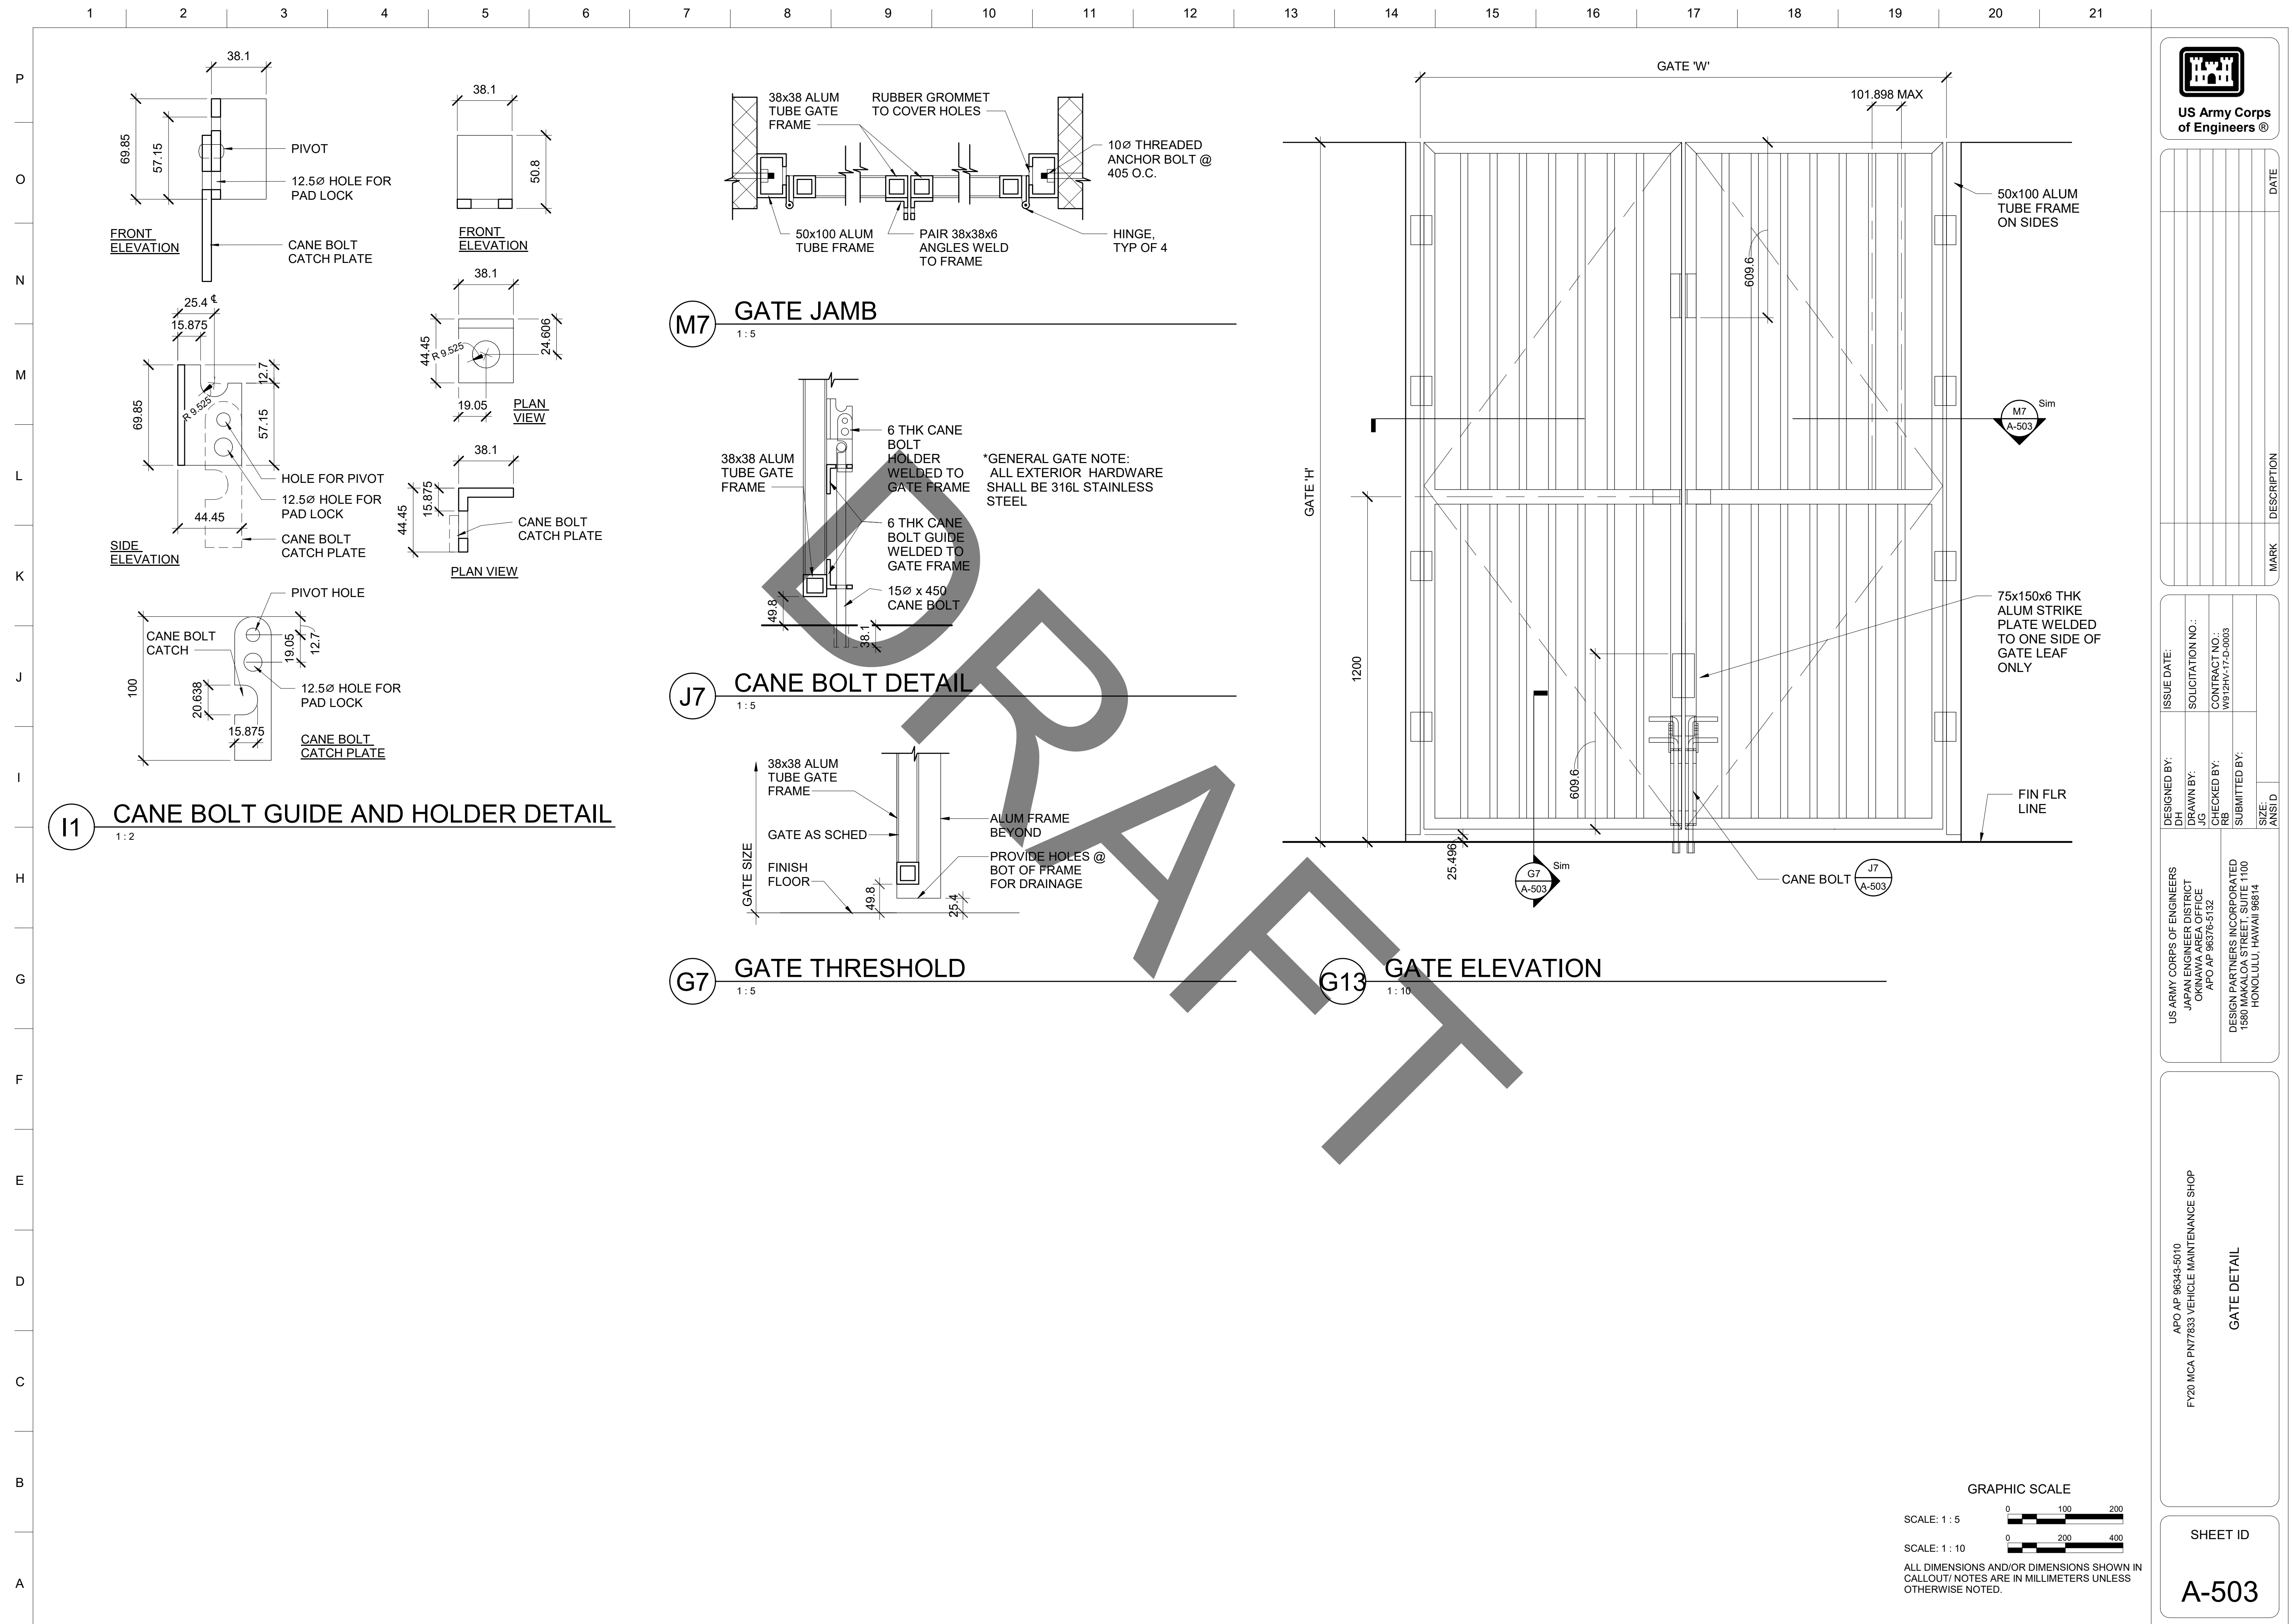


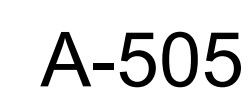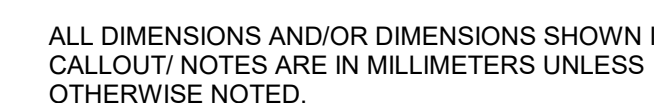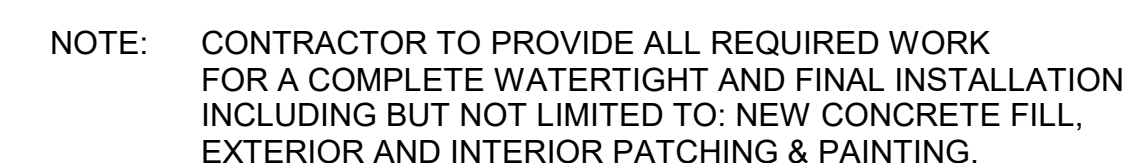

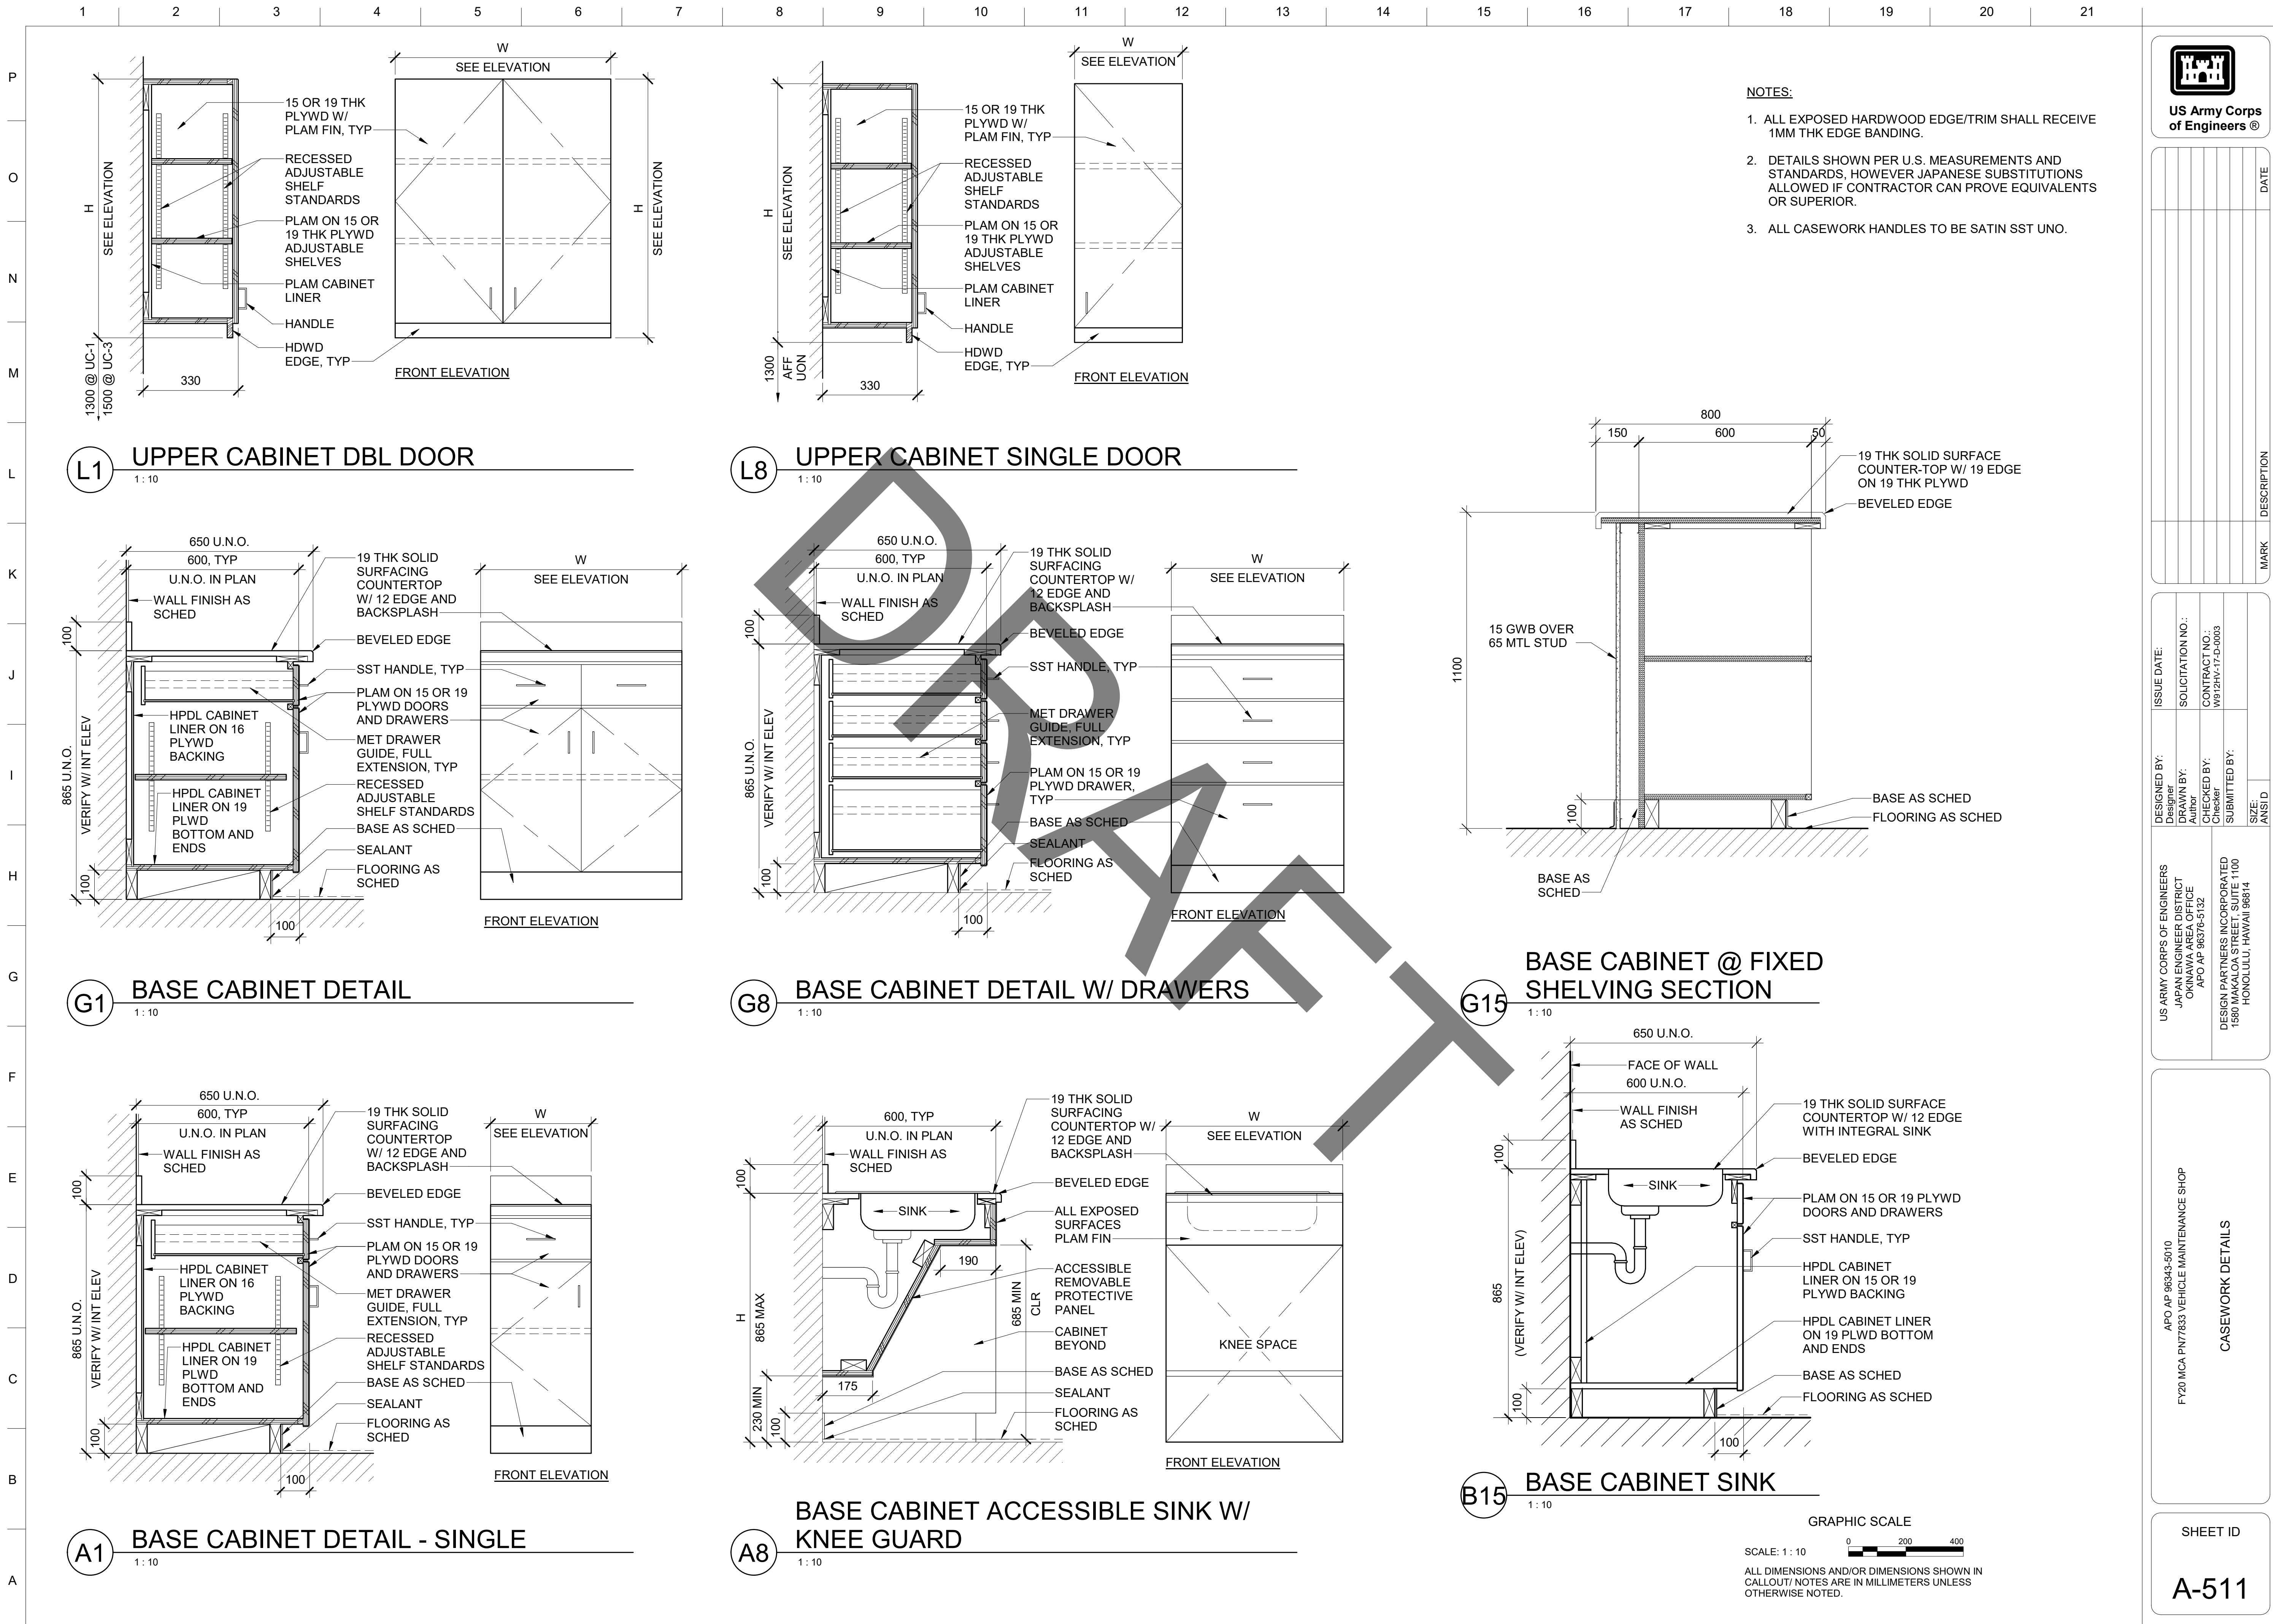


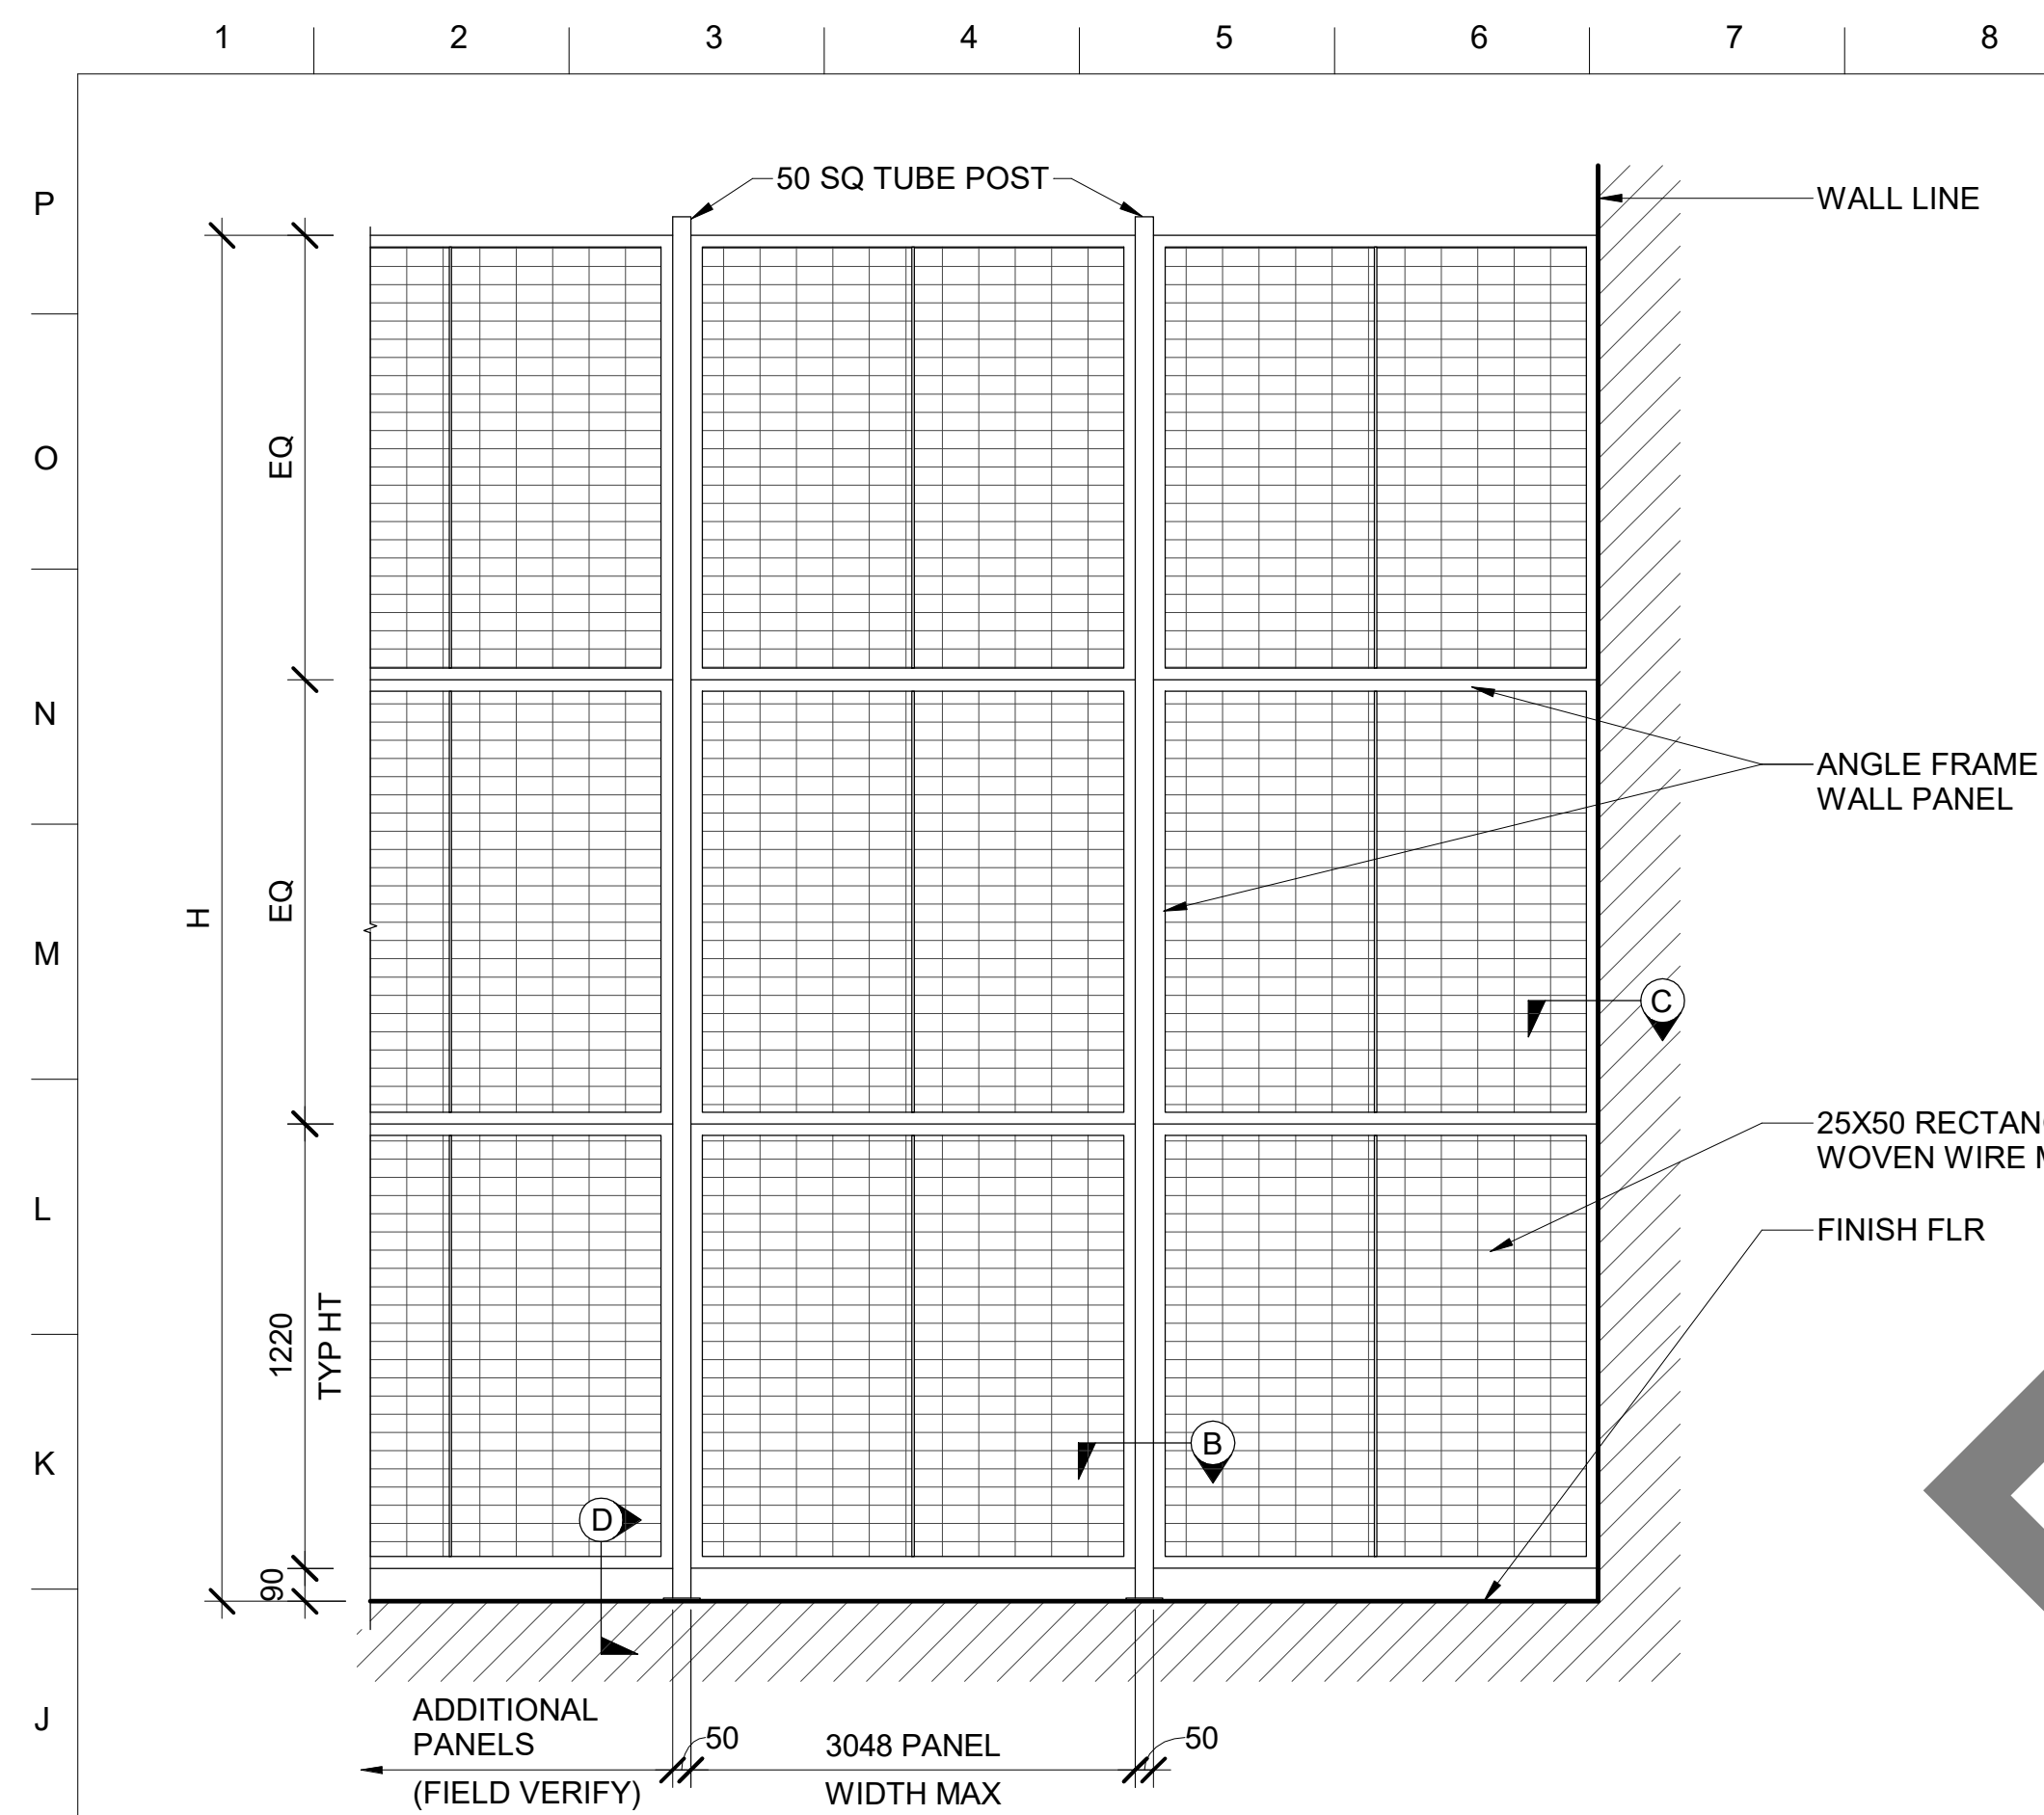


11 WIRE MESH PARTITION ELEVATION

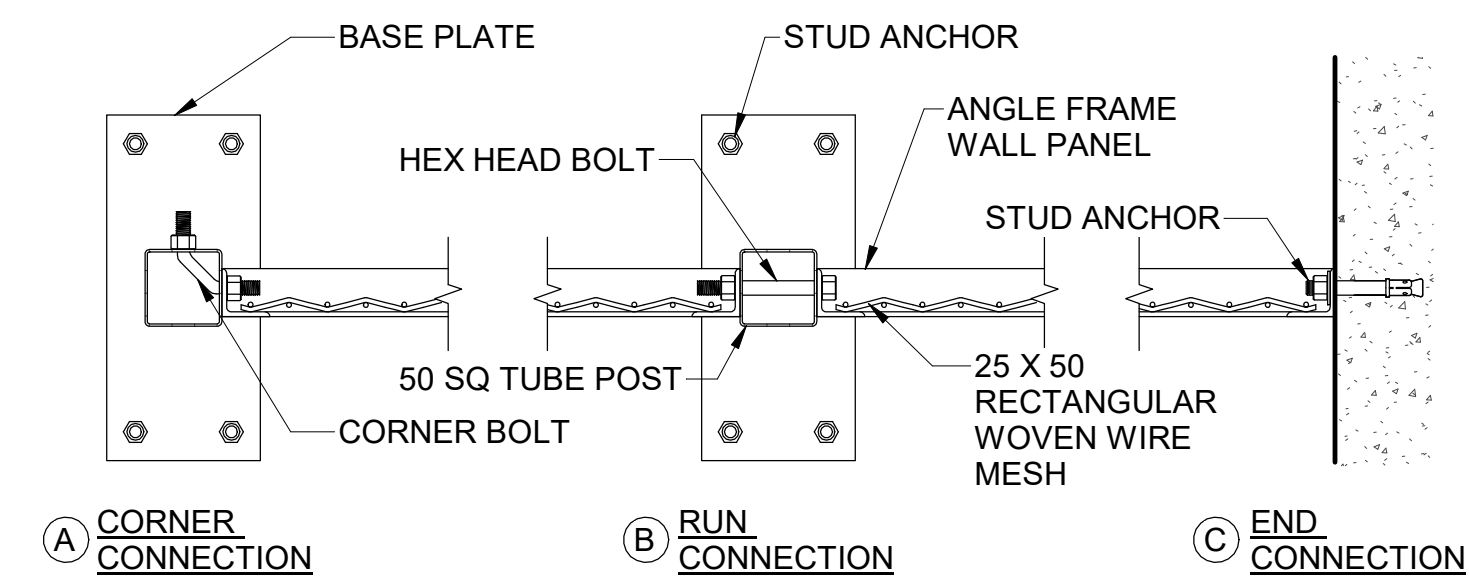

(M9) WIRE MESH PARTITION DETAIL
1:5

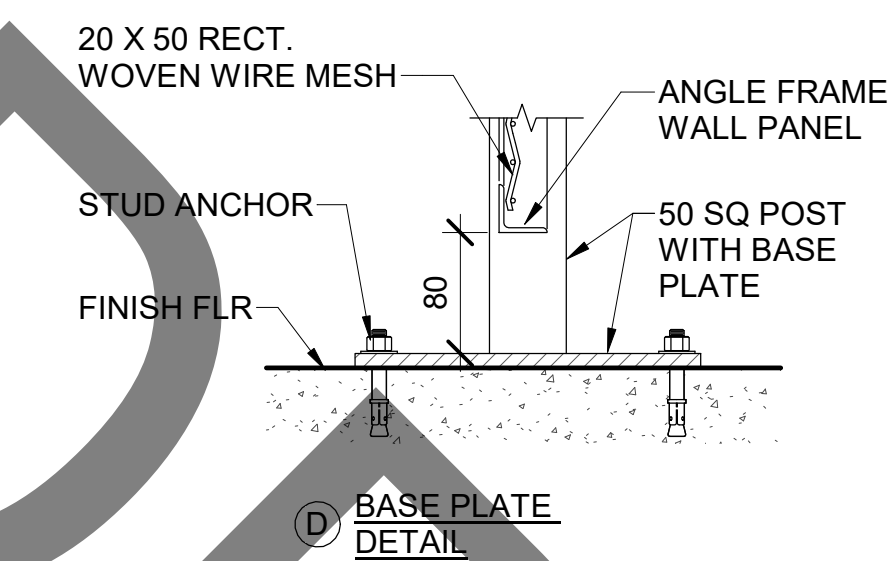

19 WIRE MESH PARTITION SECTION
1:5

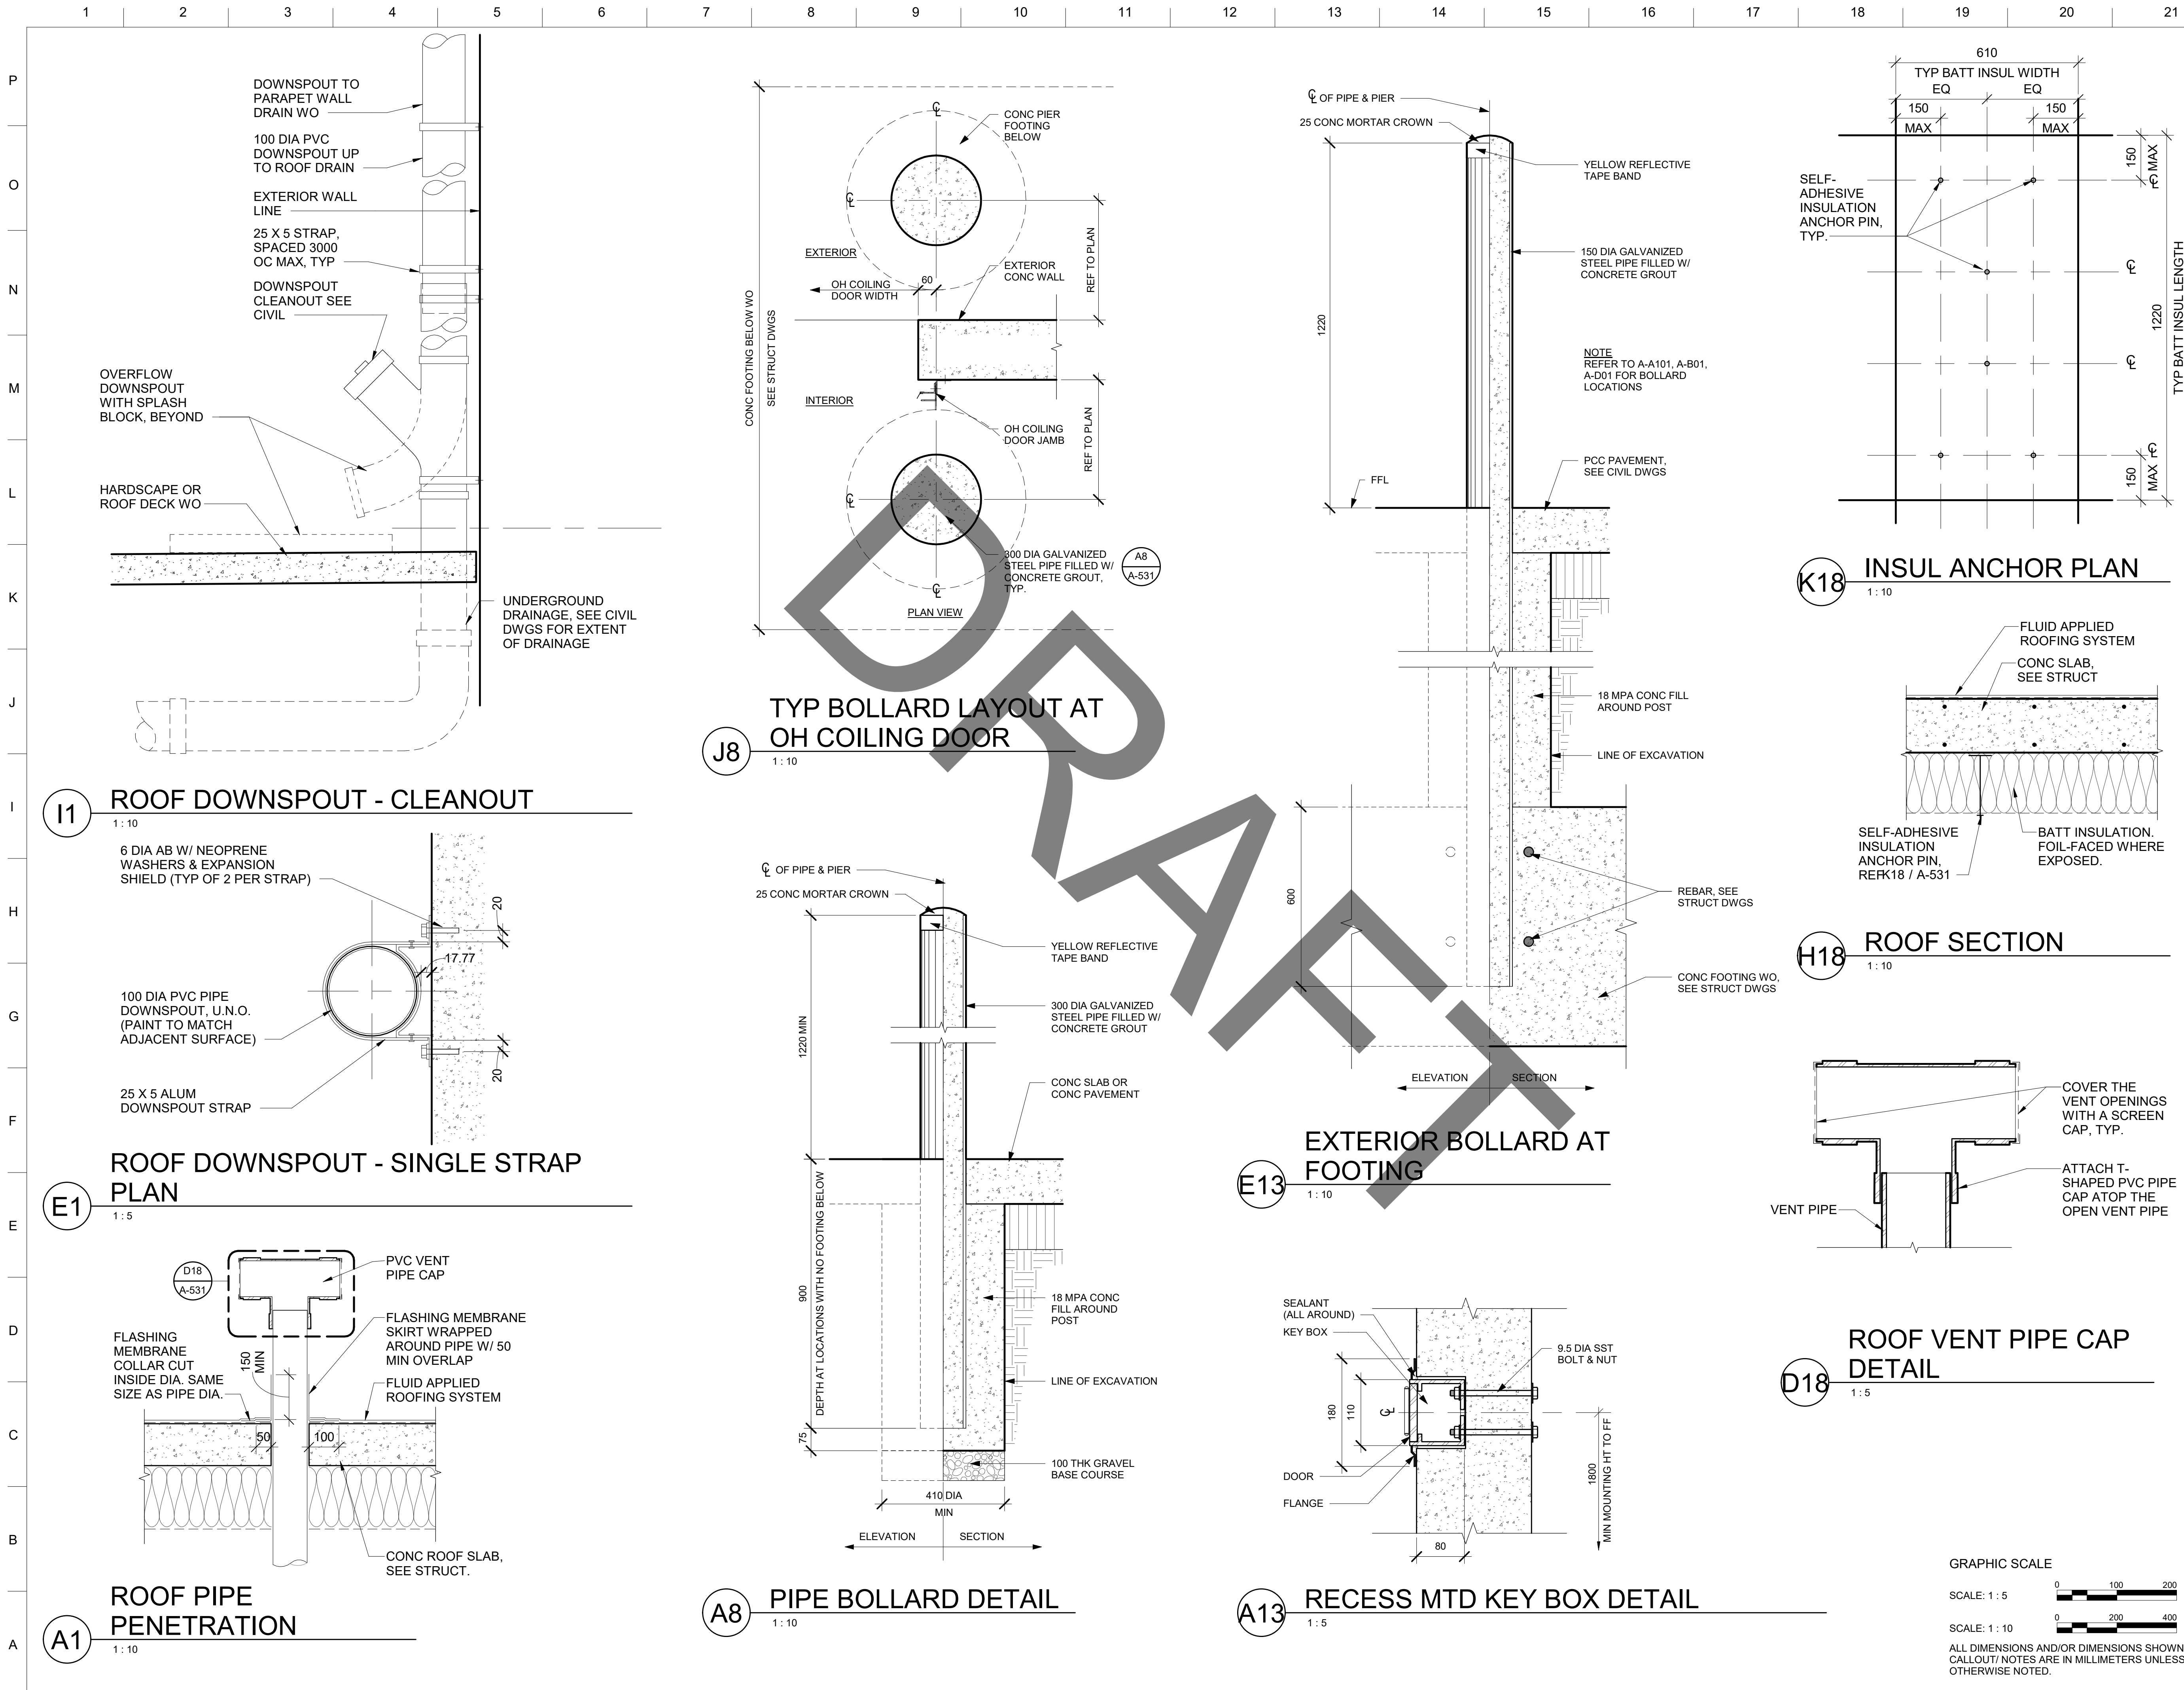

US Army Corps of Engineers

MARK	DESCRIPTION	DATE
		21 JUN 2023

DESIGNED BY: Designer JAPANESE ENGINEERING DISTRICT OKINAWA AREA OFFICE APO AP 96376-5132	ISSUE DATE:
DRAWN BY: Author OKINAWA AREA OFFICE APO AP 96376-5132	SOLICITATION NO.:
CHECKED BY: Checked OKINAWA AREA OFFICE APO AP 96376-5132	CONTRACT NO.:
SUBMITTED BY: Submitted OKINAWA AREA OFFICE APO AP 96376-5132	W9124V-17-D-0003
SIZE: ANSI D	


US ARMY CORPS OF ENGINEERS JAPANESE ENGINEERING DISTRICT OKINAWA AREA OFFICE APO AP 96376-5132	DESIGN PARTNERS INCORPORATED 1580 MAKALOA STREET, SUITE 1100 HONOLULU, HAWAII 96814
---	---

EXTERIOR DETAILS
SHEET ID
A-531

Autodesk Docs/SPIN/RED DC VEHICLE MAINTENANCE SHOP/17795_TEMF_ARCH_V02214

Plot Date: 12/17/2025 5:17:55 AM
File Path:

INTERMEDIATE DESIGN

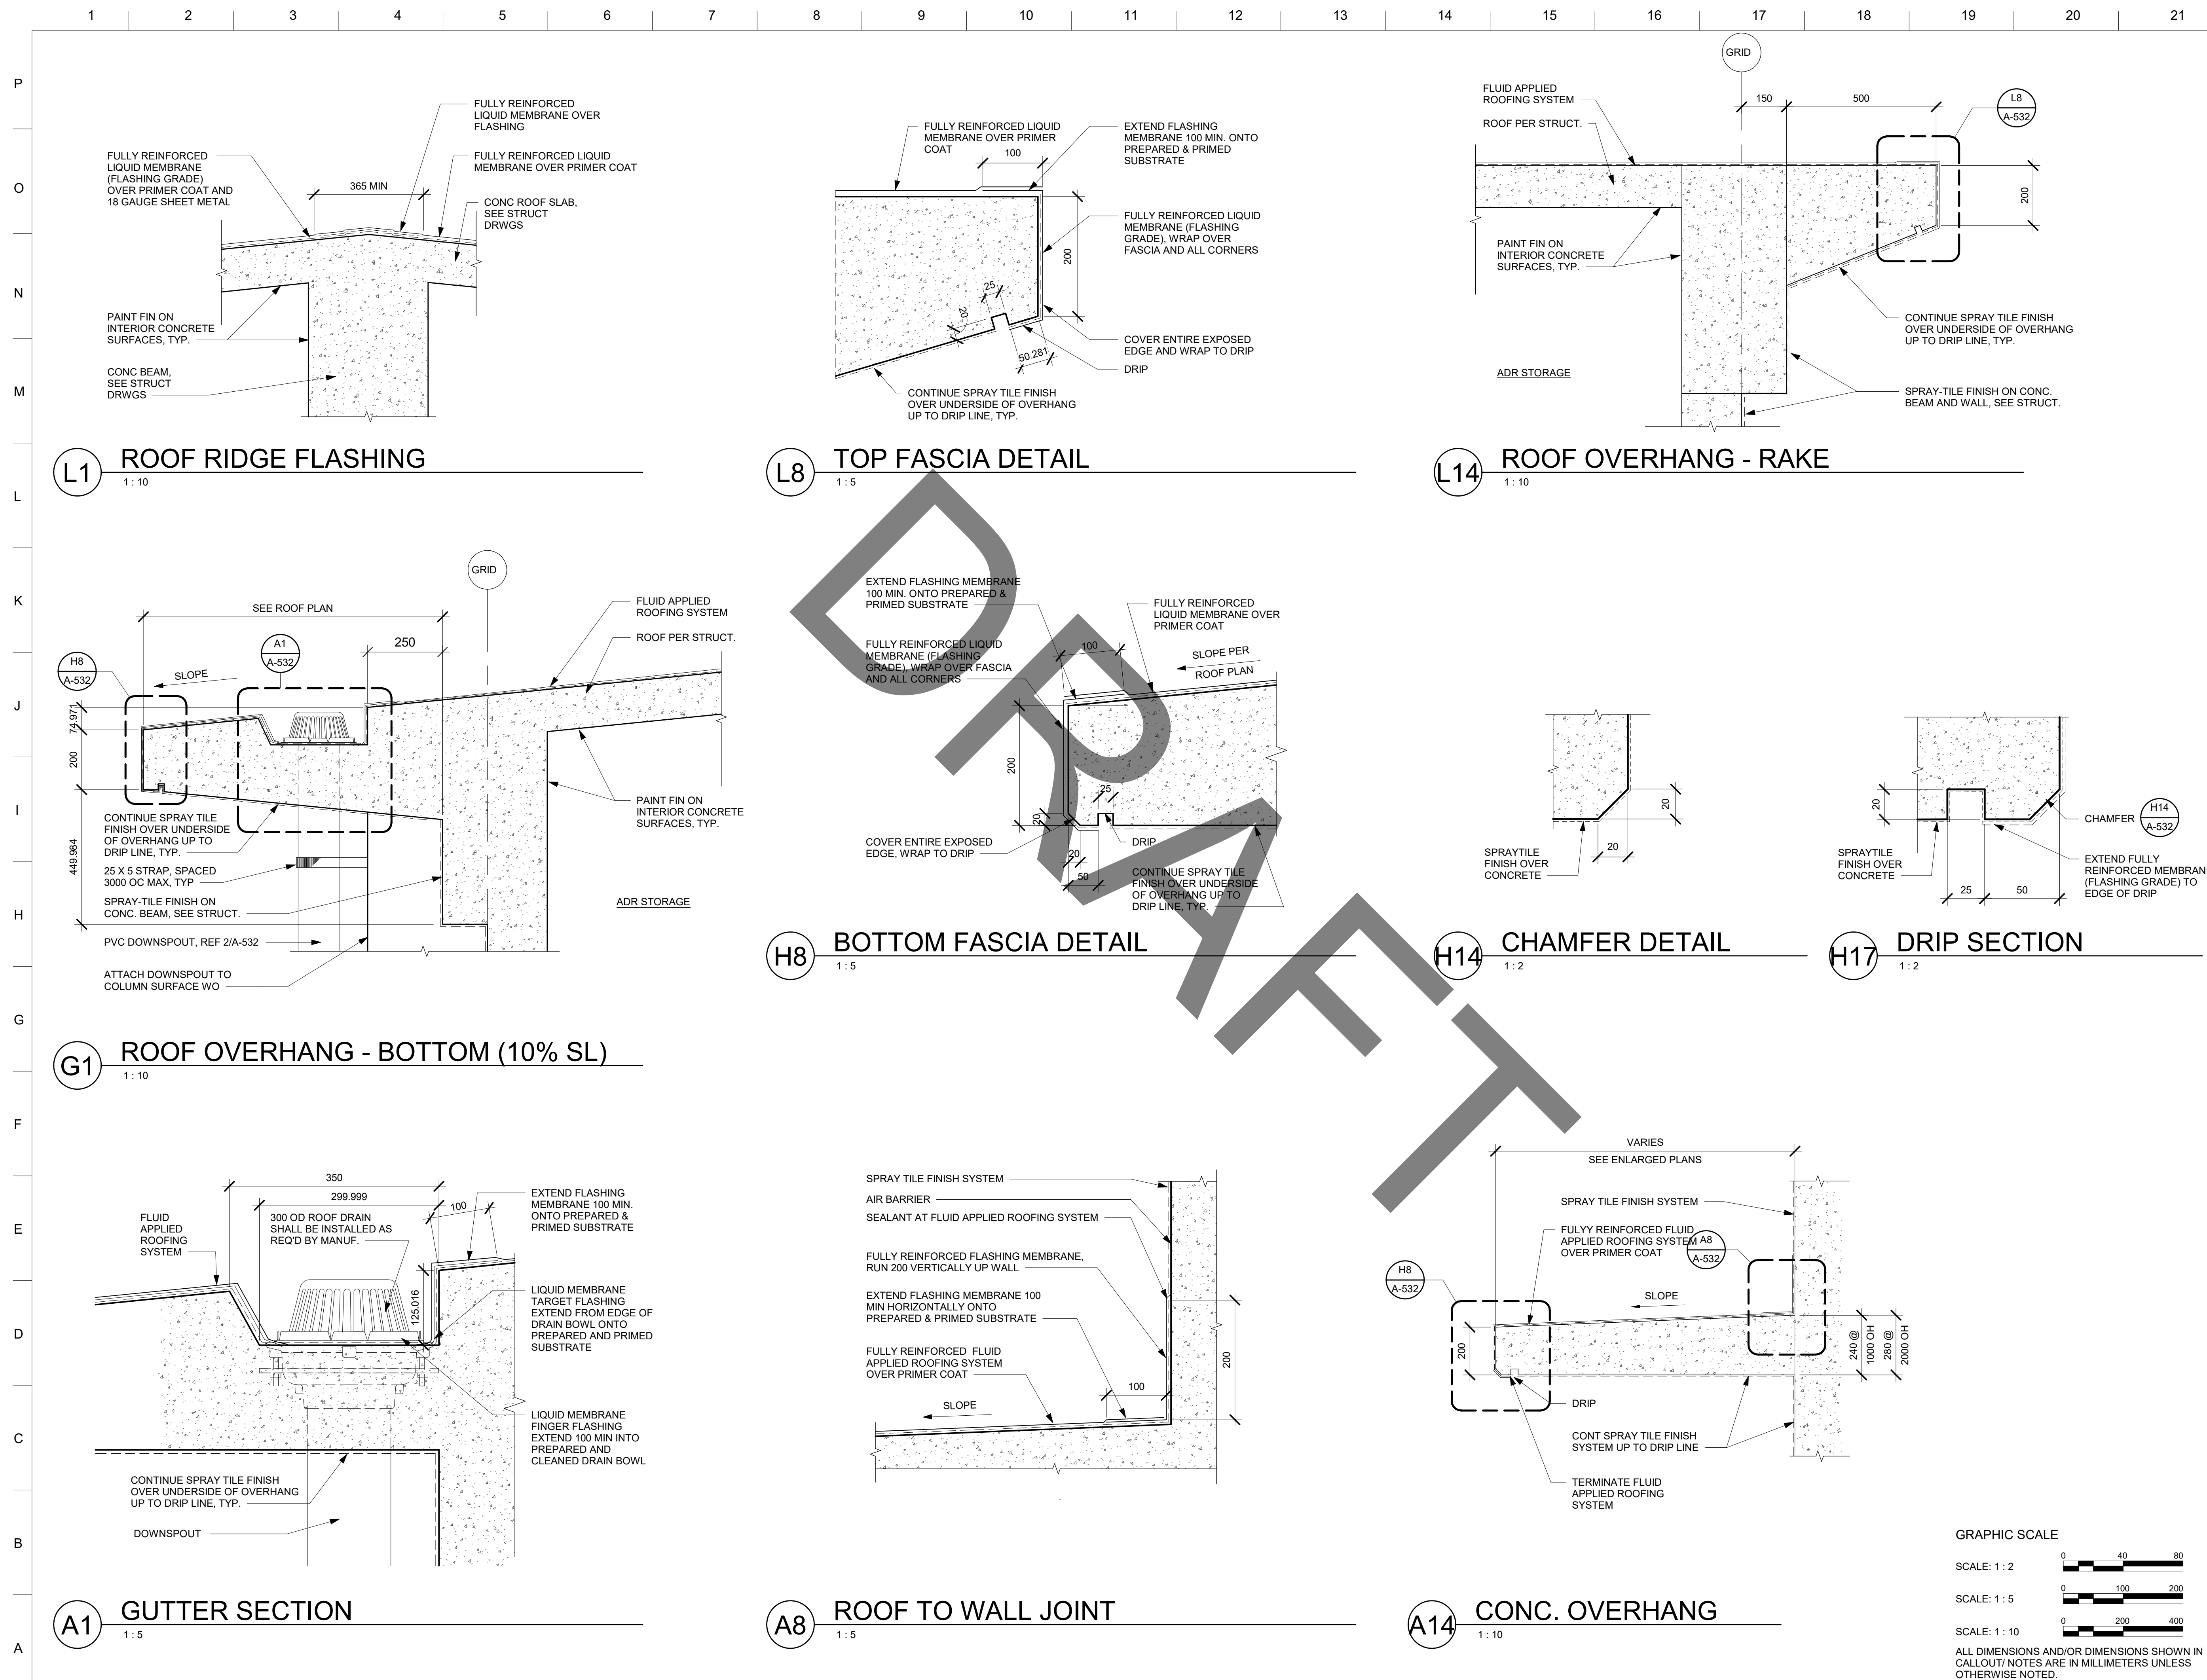
[illegible]

US ARMY CORPS OF ENGINEERS JAPAN ENGINEERS DISTRICT AFWA AREA OFFICE APO AF 96376-5132	DESIGNED BY: KELLINGWOOD	ISSUE DATE:
DESIGN PARTNERS INCORPORATED 1580 KALANANU'U BLVD, SUITE 1100 HONOLULU, HAWAII 96814	DRAWN BY: ALEX J MANUUA	SOLICITATION NO.:
	RECHECK BY: D MCATS	CONTRACT NO.:
	SUBMITTED BY:	W912HV-17-D-0003
SIZE:	DATE:	


APO AP 96343-5010
FY20 MCA PN77833 VEHICLE MAINTENANCE SHOP
EXTERIOR DETAILS

SHEET ID


A-532

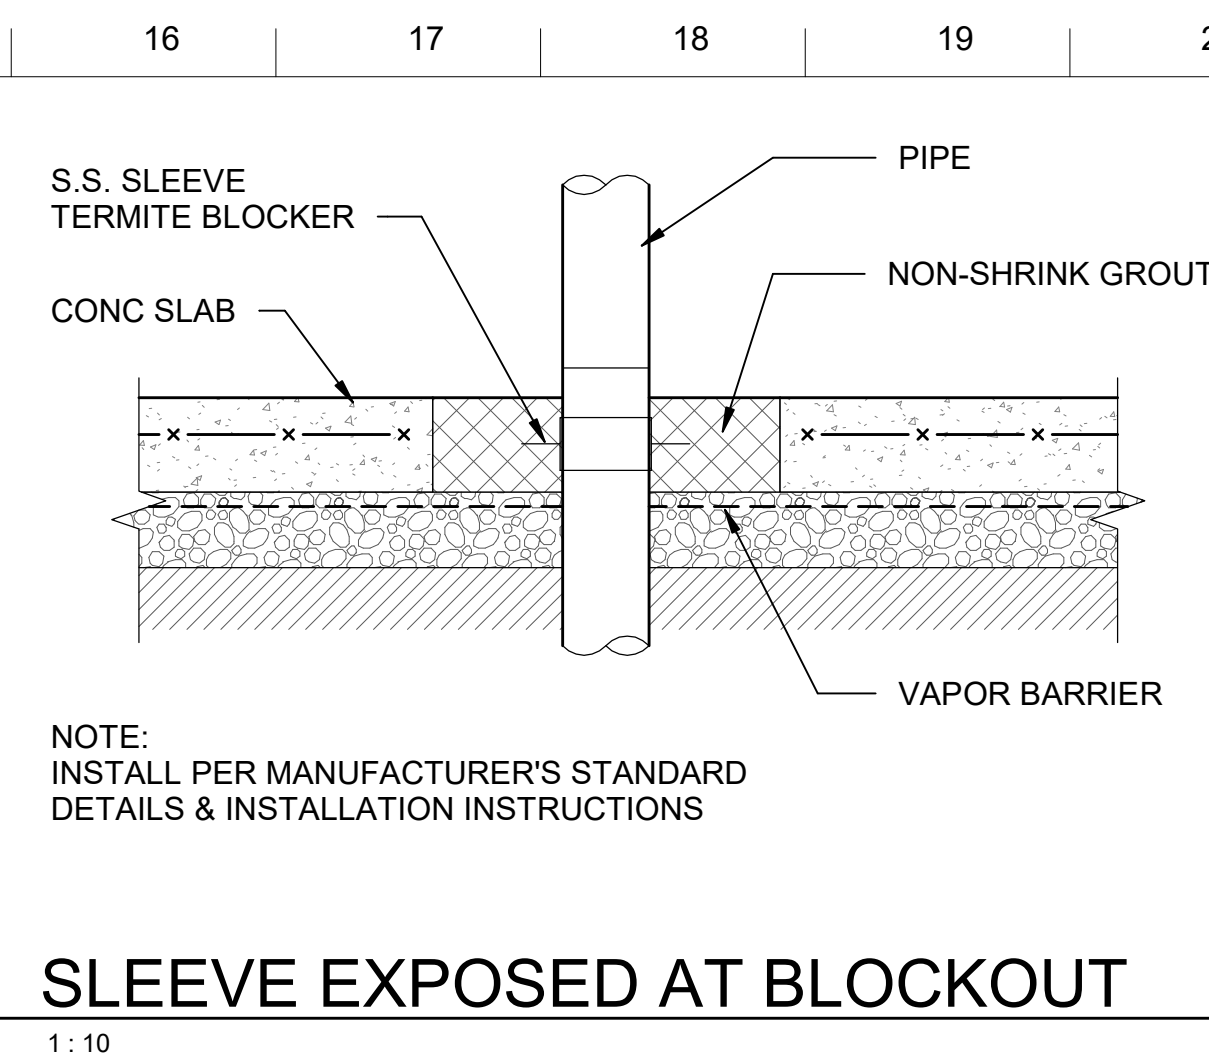


M15 SLEEVE EXPOSED AT BLOCKOUT
1:10

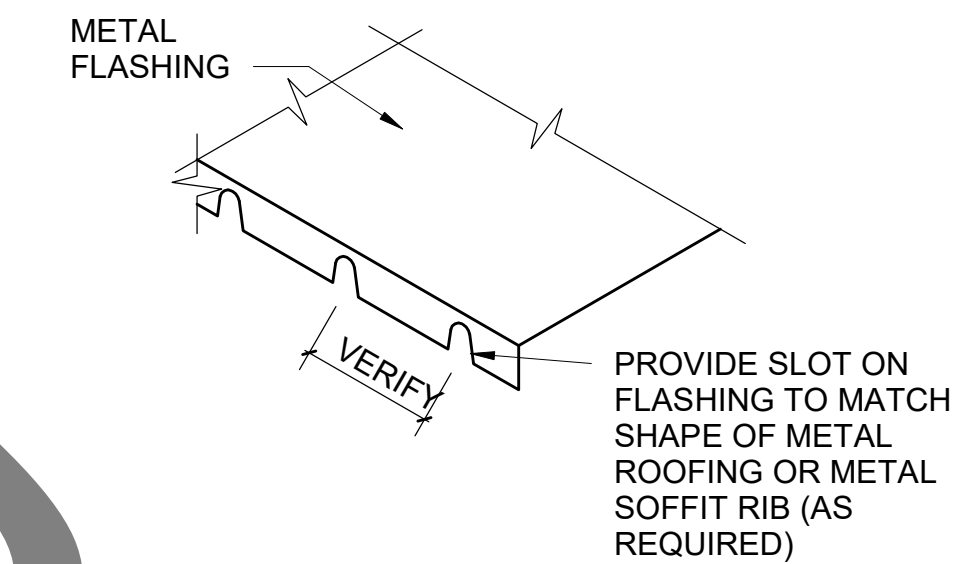


J11 SLOT FLASHING DETAIL

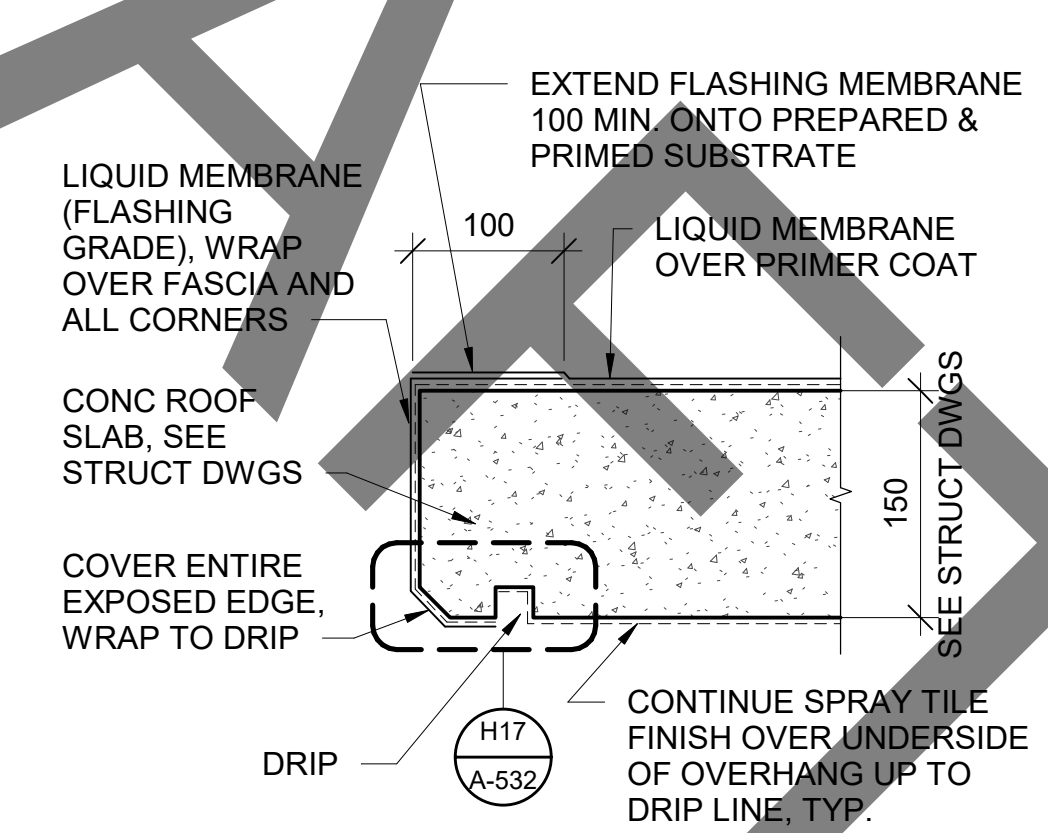


F11 RAKE FASCIA

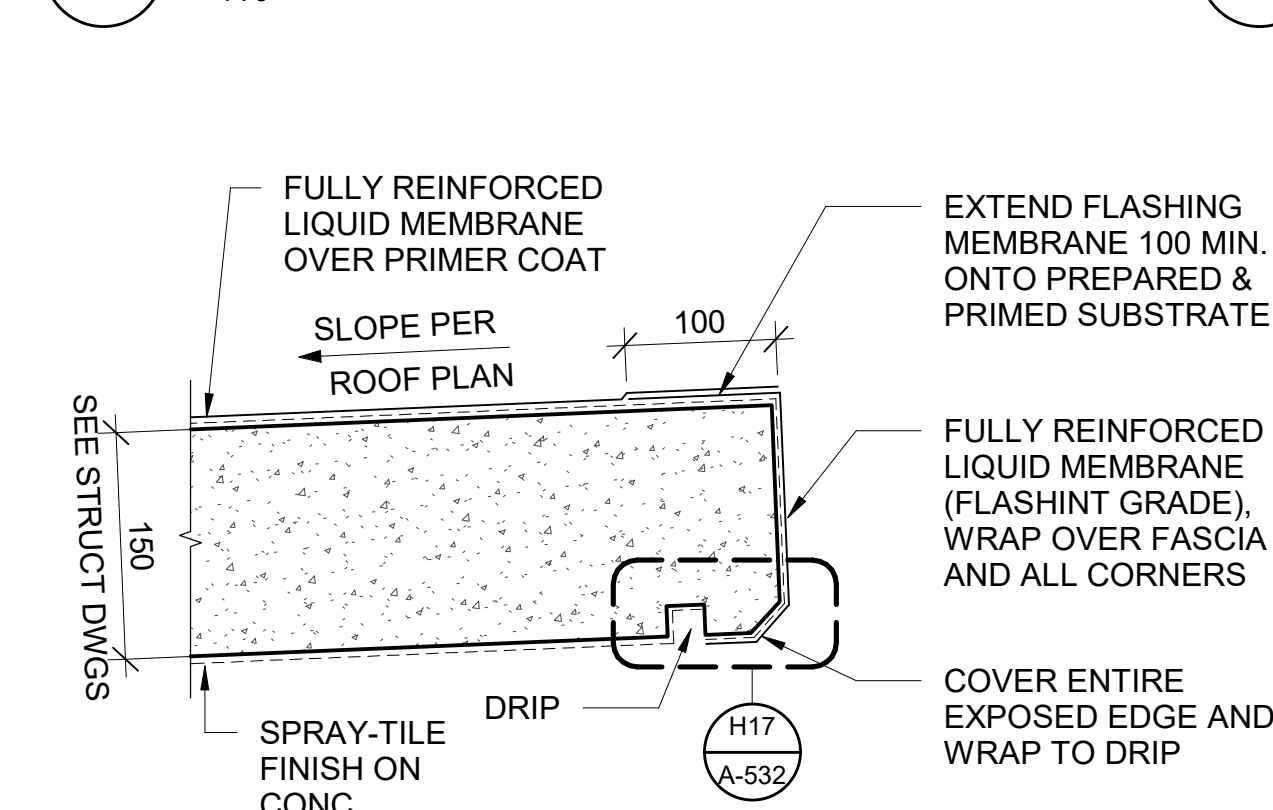

A7 TOP FASCIA - LOW SLOPE

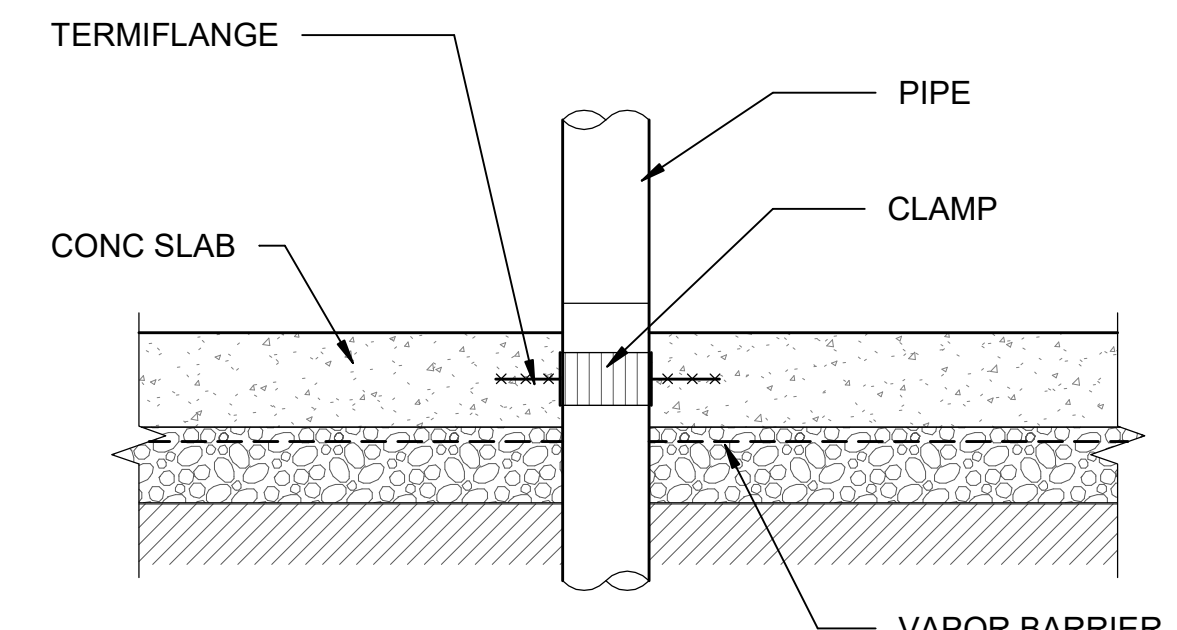



H15 TERMITE MESH @ PIPE PENETRATION

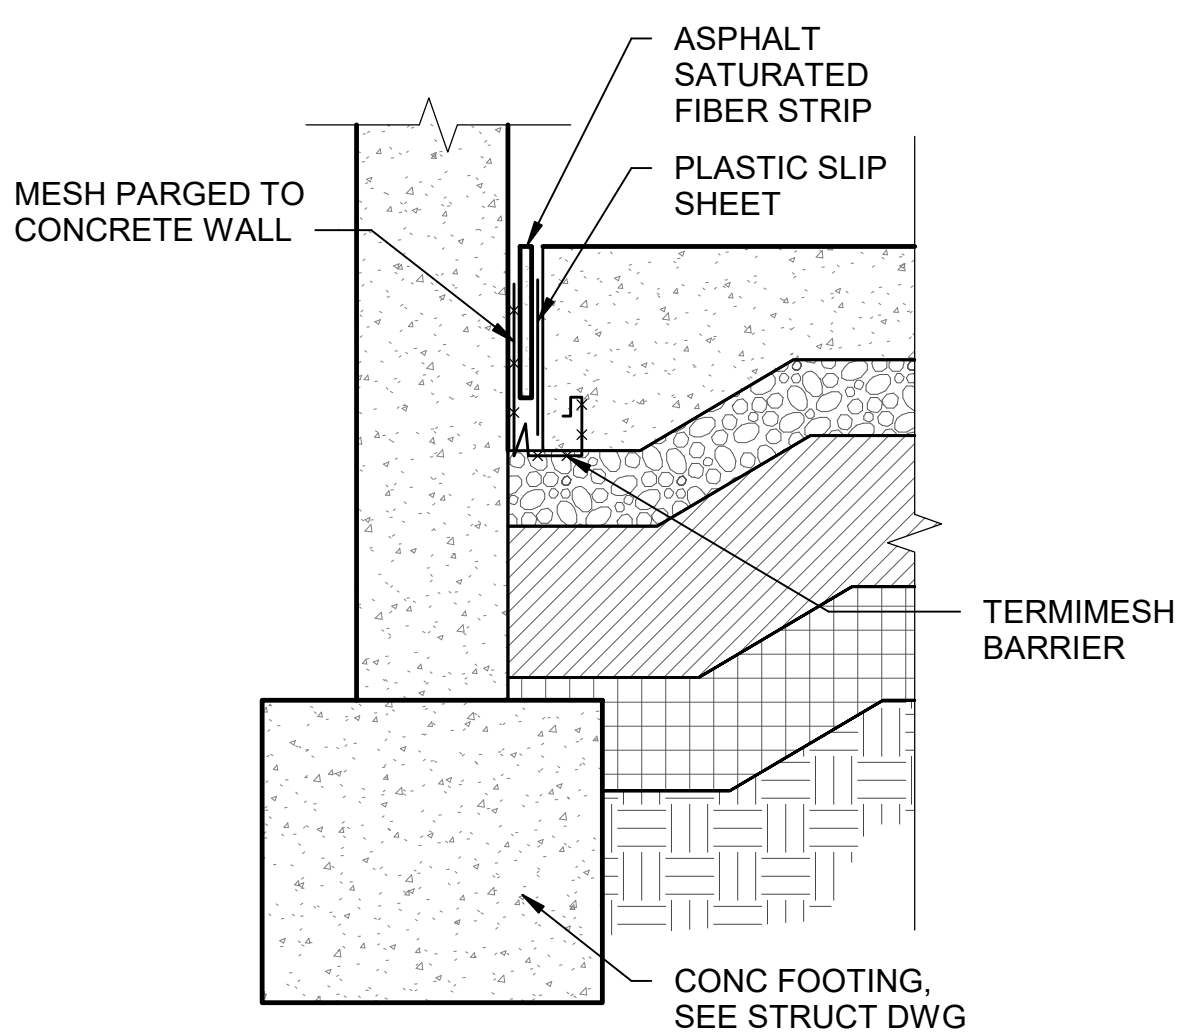

TERMITE MESH @ THICKENED SLAB
EDGE DETAIL

NOTE: CONTRACTOR TO PROVIDE ALL REQUIRED WORK FOR A COMPLETE WATERTIGHT AND FINAL INSTALLATION INCLUDING BUT NOT LIMITED TO: NEW CONCRETE FILL, EXTERIOR AND INTERIOR PATCHING & PAINTING.

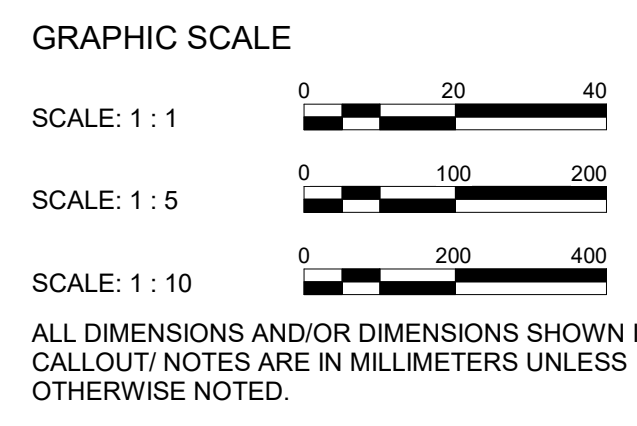


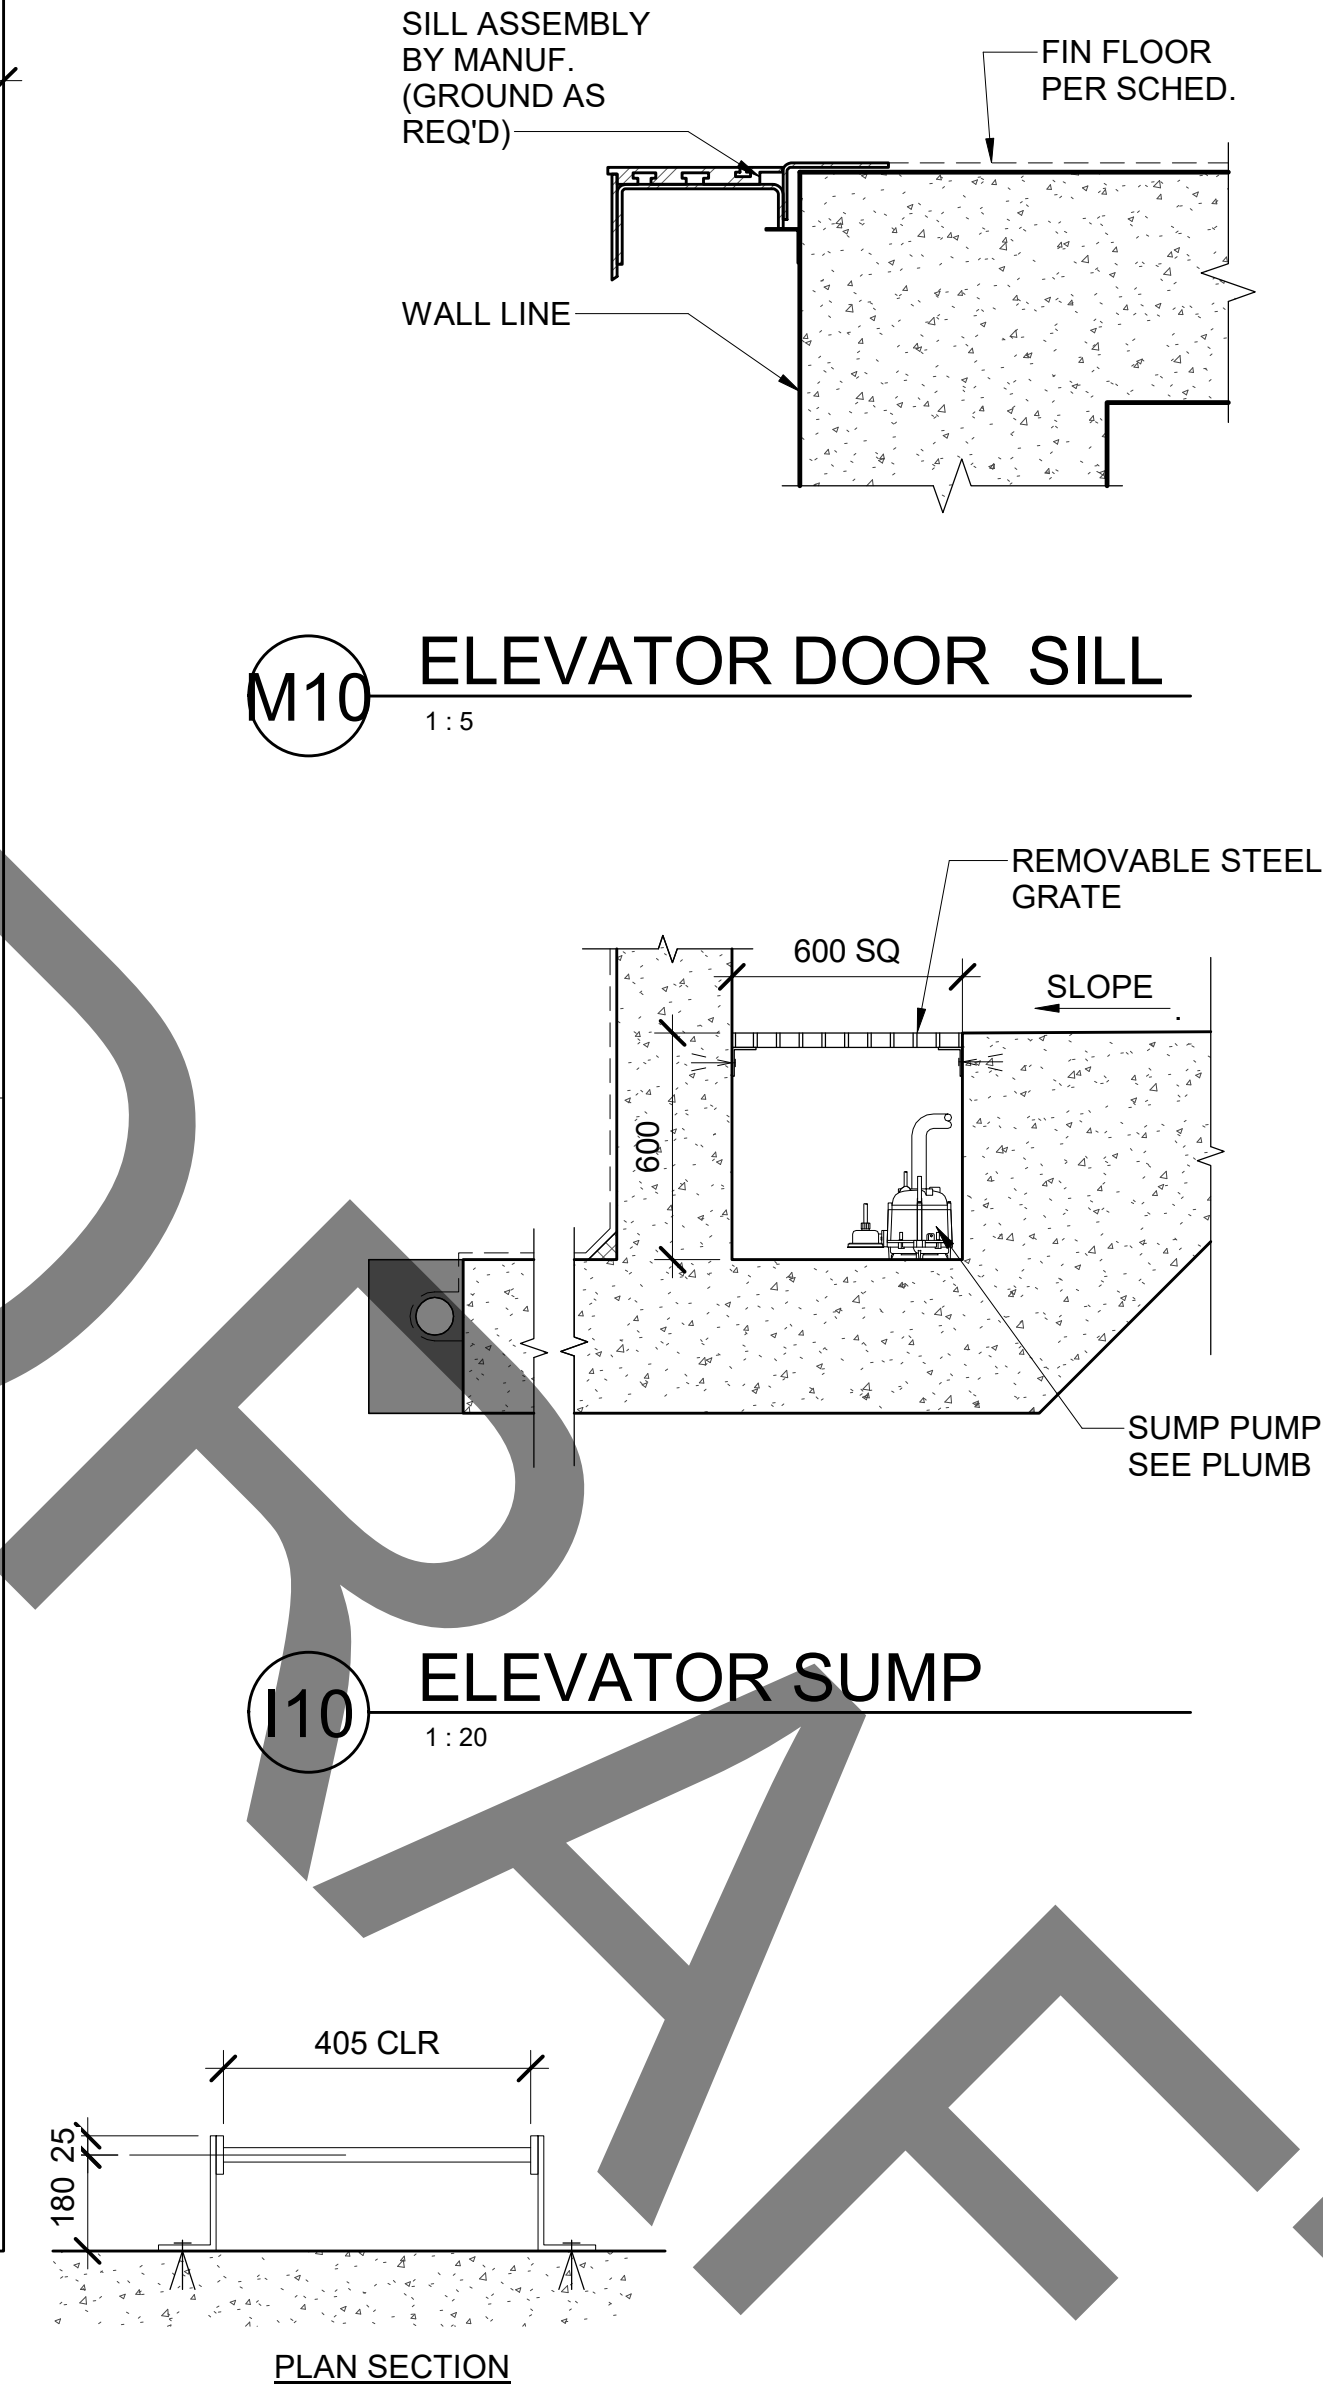


NOTE:

1. STEEL SHALL BE HOT DIPPED GALVANIZED.
2. VERIFY CLEARANCES WITH ELEVATOR MANUF.

I10 ELEVATOR SUMP

NOTE: CONTRACTOR TO PROVIDE ALL REQUIRED WORK FOR A COMPLETE WATERTIGHT AND FINAL INSTALLATION INCLUDING BUT NOT LIMITED TO: NEW CONCRETE FILL, EXTERIOR AND INTERIOR PATCHING & PAINTING.

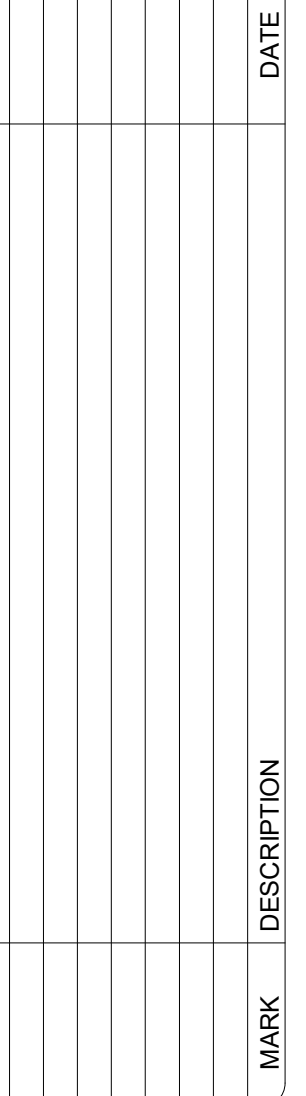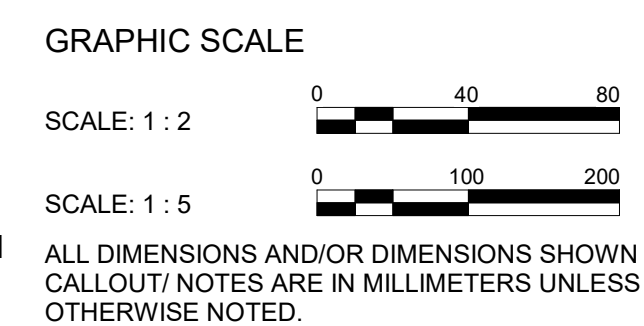

US ARMY CORPS OF ENGINEERS ENGINEERING DISTRICT OKINAWA AREA ENGINEERING CENTER APO AF 96376-5132	K ELLINGWOOD DRAWN BY: TROLLO, J MANUIA CHECKED BY: D MOATS SUBMITTED BY:	SOLICITATION NO.: CONTRACT NO.: W9124W-17-D-0003
DESIGN PARTNERS INCORPORATED 1580 KALANANULANI BLVD #1100 HONOLULU, HAWAII 96814	SIZE: ANSI/D	

MISCELLANEOUS DETAILS

A-534



ALL DIMENSIONS AND/OR DIMENSIONS SHOWN IN
CALLOUT/ NOTES ARE IN MILLIMETERS UNLESS
OTHERWISE NOTED.



--	--	

	DOOR / GATE SCHEDULE - SS (CLIN 0004)																				
K	DOOR NO.	ROOM NAME			TYPE	SIZE			DOOR		FRAME		GLAZING TYPE	FIRE/SMOKE RATING	HARDWARE	DETAILS			STC RATING	COMMENTS	
	E101	UNSERVICEABLE BULK STORAGE			J	4200	2100	40	CL	GALV	MTL	GALV		-	HW 1.0						

1. (-) = INDICATES FEATURE NOT REQUIRED.
2. DOOR / GATE TYPES: SCHEDULE
SEE DOOR TYPES
3. THICKNESS:
85, 45, 25, ETC = THICKNESS IN MILLIMETERS
4. DOOR / GATE CONSTRUCTION:
HM = HOLLOW METAL
AL = ALUMINUM
STL = STEEL
EMM = EXPANDED METAL MESH
CL = CHAIN LINK
WD = WOOD, SOLID CORE
5. FRAME CONSTRUCTION:
HM = HOLLOW METAL
AL = ALUMINUM
STL = STEEL
MTL = METAL
6. GLASS & LOUVER:
VP = VISION PANEL LAMINATED GLAZING
7. FACING & FINISH:
MP = METAL, PAINTED
AF = CLEAR ANODIZED ALUMINUM FINISH
MFR = INSTALL PER MANUFACTURER'S INSTRUCTIONS
GALV = GALVANIZED
WM = WIRE MESH
WMP = WOOD, PAINTED
8. RATING:
(-) = NO RATING REQUIRED
45, 60, ETC = FIRE RATING IN MINUTES
S = NON-RATED SMOKE RESISTANT
9. HARDWARE GROUP SET:
SEE SPECIFICATIONS
10. REMARKS:
1. PROVIDE DOOR CLOSURE
2. PROVIDE PANIC HARDWARE
3. PROVIDE KICK PLATE
4. PROVIDE DOOR SEAL AND GASKET THRESHOLD
5. PROVIDE PRIVACY LOCK
6. VAULT DOOR ACTUAL THICKNESS PER MANUFACTURE SPECIFICATION FOR CLASS 5 VAULT DOOR.
7. HEAVY DUTY METAL DOOR - 10GA SHEET METAL ON 4 PLY WOOD DOOR, AND 18GA FACE METAL LAYER.

DOOR / GATE TYPES

A FLUSH PANEL, SWING DOOR

A2 FLUSH PANEL W/ LOUVER, SWING DOOR

AA PAIR FLUSH PANEL, SWING DOOR

B FLUSH W/ VISION PANEL, SWING DOOR

BB PAIR FLUSH W/ VISION PANEL, SWING DOOR

BB2 PAIR FLUSH W/ LARGE VISION PANEL, SWING DOOR

C VAULT DOOR W/ DUTCH DOOR DAY GATE AND SERVING WINDOW

D OPERABLE PARTITION

E PAIR WIRE MESH, SWING GATE

F OVERHEAD COILING DOOR

G OVERHEAD SECTIONAL DOOR

H LOCKABLE COUNTERTOP SHUTTER

I PAIR PICKET, SWING GATE

J PAIR CHAIN LINK, SWING GATE

GENERAL DOOR NOTES

1. DESIGN BLAST DOORS IN ACCORDANCE WITH:
a. UFC 4-010-01 DOD MINIMUM ANTITERRORISM STANDARDS FOR BUILDINGS, 1OCTOBER 2013 WITH CHANGE 1
b. UFC 4-010-02 DOD MINIMUM ANTITERRORISM STANDOFF DISTANCES FOR BUILDINGS, 9 FEBRUARY 2012
c. SPECIFIED WIND AND BLAST LOADS

2. EXTERIOR BLAST RESISTANT DOORS SHALL BE TESTED TO ACHIEVE THE APPLICABLE PERFORMANCE IN UFC 4-010-01, TABLE 2-1 IN ACCORDANCE WITH ASTM F2247 (UNGLAZED DOORS) OR ASTM F2927 (GLAZED DOOR). THE BLAST PROTECTION CRITERIA FOR THE DESIGN OF EXTERIOR DOORS ARE AS FOLLOWS:
a. REQUIRED DOOR HAZARD RATING: CATEGORY IV SEVERE DEFORMATION. DOOR PANEL IS SEVERELY DEFORMED WITH OPENINGS BETWEEN THE DOOR AND FRAME, BUT THE DOOR REMAINS AFFIXED TO THE FRAME
b. REQUIRED DOOR REBOUND RESPONSE: 0%, NO REBOUND RESPONSE
c. FOR DYNAMIC AIR-BLAST TESTING, THE APPLICABLE PEAK BLAST PRESSURE IS ____ kPa. THIS VALUE CORRESPONDS TO THE UNOBSTRUCTED ZONE STANDOFF DISTANCE OF ____ METERS AND EXPLOSIVE WEIGHT TYPE II

3. ARMORY VAULT DOOR SHALL BE GSA-APPROVED CLASS 5 WITH LOCK IN ACCORDANCE WITH FED. SPEC. AA-D-600D

US Army Corps of Engineers ®

ISSUE DATE:

SOLICITATION NO.:

CONTRACT NO.:

MARK

DATE

DESIGNED BY: KELLINGWOOD

DRAWN BY: IROLLO, J. MANUJA

CHECKED BY: W/12AV-17-D-0003

SUBMITTED BY: ANSI/D

SIZE: ANSI/D

US ARMY CORPS OF ENGINEERS
JAPAN ENGINEER DISTRICT
OKINAWA AREA OFFICE
APO AP 96376-5132

DESIGN PARTNERS INCORPORATED
1580 MAKALOA STREET, SUITE 1100
HONOLULU, HAWAII 96814

APO AP 96343-5010
FY20 MCA PN77833 VEHICLE MAINTENANCE SHOP

DOOR & GATE SCHEDULE (CLIN 0002 & CLIN 0004), TYPES AND NOTES

SHEET ID

A-602

INTERMEDIATE DESIGN

Autodesk Docs/ISSUED DC VEHICLE MAINTENANCE SHOP151795_TEMPL_ARCT_002214

Plot Date: 12/17/2025 5:18:07 AM

File Path:

DOOR / GATE SCHEDULE - COF SS (CLIN 0004)																		
DOOR NO.	ROOM NAME	TYPE	SIZE			DOOR		FRAME		GLAZING TYPE	FIRE/SMOKE RATING	HARDWARE	DETAILS			STC RATING	COMMENTS	
			W	HT	THK	MAT	FIN	MAT	FIN				HEAD	JAMB	THRESHOLD			
H100	MECH YARD	Z	3600	2100	50	AL	AF	AL	AF		-	HW1.0	G13/A-503	M7/A-503	G7/A-503			
H101	HALL	A	900	2100	45	WD	WP	HM	WP		-	HW 7.0	I1/A-501	I1/A-501	E1/A-501			
H102	MEN'S TOILET	A	900	2100	45	WD	WP	HM	WP		-	HW 40.0	M17/A-501	M17/A-501	E7/A-501			
H103	WOMEN'S TOILET	A	900	2100	45	WD	WP	HM	WP		-	HW 40.0	M17/A-501	M17/A-501	E7/A-501			
H104	JANITOR	A	900	2100	45	HM	MP	HM	MP		-	HW 32.0	M17/A-501	M17/A-501	E7/A-501			
H105	TELECOM	AA	1800	2100	45	WD	WP	HM	WP		-	HW 8.0	M17/A-501	M17/A-501	I17/A-501			
H106	ELEC	AA	1800	2100	45	AL	AF	AL	AF		-	HW 4.0	I1/A-501	I1/A-501	E1/A-501			
H110	VEST	AA	1800	2100	45	AL	AF	AL	AF		-	HW 2.0	I1/A-501	I1/A-501	E1/A-501			
H111	STORAGE	AA	1800	2100	45	WD	WP	HM	WP		-	HW 12.0	M17/A-501	M17/A-501	E7/A-501			
H112	CLASSROOM	AA	1800	2100	45	WD	WP	HM	WP		-	HW 13.0	M17/A-501	M17/A-501	E7/A-501			
H113	OFFICE	A	900	2100	45	WD	WP	HM	WP		-	HW 19.0	M17/A-501	M17/A-501	E7/A-501			
H120	ENTRY	AA	1800	2100	45	AL	AF	AL	AF		-	HW 2.0	I1/A-501	I1/A-501	E1/A-501			
H123	CO OFFICE	A	900	2100	45	WD	WP	HM	WP		-	HW 23.0	M17/A-501	M17/A-501	I7/A-501			
H124	1ST SGT OFFICE	A	900	2100	45	WD	WP	HM	WP		-	HW 23.0	M17/A-501	M17/A-501	I7/A-501			
H125	XO OFFICE	A	900	2100	45	WD	WP	HM	WP		-	HW 23.0	M17/A-501	M17/A-501	I7/A-501			
H126	STOR	A2	900	2100	45	WD	WP	HM	WP		-	HW 26.0	M17/A-501	M17/A-501	E7/A-501			
H127	COMM STOR	A2	900	2100	45	WD	WP	HM	WP		-	HW 26.0	M17/A-501	M7/A-501	E7/A-501			
H130	ENTRY	AA	1800	2100	45	AL	AF	AL	AF		-	HW 2.0	I1/A-501	I1/A-501	E1/A-501			
H133	CO OFFICE	A	900	2100	45	WD	WP	HM	WP		-	HW 23.0	M17/A-501	M17/A-501	I7/A-501			
H134	1ST SGT OFFICE	A	900	2100	45	WD	WP	HM	WP		-	HW 23.0	M17/A-501	M17/A-501	I7/A-501			
H135	XO OFFICE	A	900	2100	45	WD	WP	HM	WP		-	HW 23.0	M17/A-501	M17/A-501	I7/A-501			
H136	STOR	A2	900	2100	45	WD	WP	HM	WP		-	HW 26.0	M17/A-501	M17/A-501	E7/A-501			
H137	COMM STOR	A2	900	2100	45	WD	WP	HM	WP		-	HW 26.0	M17/A-501	M17/A-501	E7/A-501			
H201	HALL	A	900	2100	45	AL	AF	AL	AF		-	HW 6.0	I1/A-501	I1/A-501	E1/A-501			
H202	MEN'S TOILET	A	900	2100	45	WD	WP	HM	WP		-	HW 40.0	M17/A-501	M17/A-501	E7/A-501			
H203	WOMEN'S TOILET	A	900	2100	45	WD	WP	HM	WP		-	HW 40.0	M17/A-501	M17/A-501	E7/A-501			
H204	JANITOR	A	900	2100	45	HM	MP	HM	MP		-	HW 32.0	M17/A-501	M17/A-501	E7/A-501			
H205	TELECOM	AA	1800	2100	45	WD	WP	HM	WP		-	HW 9.0	M17/A-501	M17/A-501	E7/A-501			
H210	ENTRY	AA	1800	2100	45	AL	AF	AL	AF		-	HW 2.0	I1/A-501	I1/A-501	E1/A-501			
H213	CO OFFICE	A	900	2100	45	WD	WP	HM	WP		-	HW 23.0	M17/A-501	M17/A-501	I7/A-501			
H214	1ST SGT OFFICE	A	900	2100	45	WD	WP	HM	WP		-	HW 23.0	M17/A-501	M17/A-501	I7/A-501			
H215	XO OFFICE	A	900	2100	45	WD	WP	HM	WP		-	HW 23.0	M17/A-501	M17/A-501	I7/A-501			
H216	COMM STOR	A2	900	2100	45	WD	WP	HM	WP		-	HW 30.0	M17/A-501	M17/A-501	I7/A-501			
H217	STOR	A2	900	2100	45	WD	WP	HM	WP		-	HW 30.0	M17/A-501	M17/A-501	I7/A-501			
H220	ENTRY	AA	1800	2100	45	AL	AF	AL	AF		-	HW 2.0	I1/A-501	I1/A-501	E1/A-501			
H223	CO OFFICE	A	900	2100	45	WD	WP	HM	WP		-	HW 23.0	M17/A-501	M17/A-501	I7/A-501			
H224	1ST SGT OFFICE	A	900	2100	45	WD	WP	HM	WP		-	HW 23.0	M17/A-501	M17/A-501	I7/A-501			
H225	XO OFFICE	A	900	2100	45	WD	WP	HM	WP		-	HW 23.0	M17/A-501	M17/A-501	I7/A-501			
H226	STOR	A2	900	2100	45	WD	WP	HM	WP		-	HW 30.0	M17/A-501	M17/A-501	I7/A-501			
H227	COMM STOR	A2	900	2100	45	WD	WP	HM	WP		-	HW 30.0	M17/A-501	M17/A-501	I7/A-501			
H230	ENTRY	AA	1800	2100	45	AL	AF	AL	AF		-	HW 2.0	I1/A-501	I1/A-501	E1/A-501			
H233	CO OFFICE	A	900	2100	45	WD	WP	HM	WP		-	HW 23.0	M17/A-501	M17/A-501	I7/A-501			
H234	1ST SGT OFFICE	A	900	2100	45	WD	WP	HM	WP		-	HW 23.0	M17/A-501	M17/A-501	I7/A-501			
H235	XO OFFICE	A	900	2100	45	WD	WP	HM	WP		-	HW 23.0	M17/A-501	M17/A-501	I7/A-501			
H236	STOR	A2	900	2100	45	WD	WP	HM	WP		-	HW 30.0	M17/A-501	M17/A-501	I7/A-501			
H237	COMM STOR	A2	900	2100	45	WD	WP	HM	WP		-	HW 30.0	M17/A-501	M17/A-501	I7/A-501			
DOOR / GATE SCHEDULE - SSAW (CLIN 0004)																		
DOOR NO.	ROOM NAME	TYPE	SIZE			DOOR		FRAME		GLAZING TYPE	FIRE/SMOKE RATING	HARDWARE	DETAILS			STC RATING	COMMENTS	
			W	HT	THK	MAT	FIN	MAT	FIN				HEAD	JAMB	THRESHOLD			
D100	MECHANICAL YARD	I	2400	2100	50	AL	AF	AL	AF		-	HW 1.0	G13/A-503	M7/A-503	G7/A-503			
D101	ENTRY	A	900	2100	45	AL	AF	AL	AF		-	HW 6.0	M1/A-501	M1/A-501	E1/A-501	49		
D102	CUSTOMER SERVICE AREA	A	900	2100	45	HM	MP	HM	MP		-	HW 18.0	M17/A-501	M17/A-501	I7/A-501	35		
D103	CLS OFFICE	A	900	2100	45	HM	MP	HM	MP		-	HW 22.0	M7/A-501	M7/A-501	I7/A-501	25		
D104	OFFICE	A	900	2100	45	HM	MP	HM	MP		-	HW 22.0	M17/A-501	M17/A-501	I7/A-501	25		
D105	STOCK CONTROL OFFICE	A	900	2100	45	HM	MP	HM	MP		-	HW 22.0	M17/A-501	M17/A-501	I7/A-501	25		
D106	OFFICE	A	900	2100	45	HM	MP	HM	MP		-	HW 22.0	M17/A-501	M17/A-501	I7/A-501	25		
D107	SIPR ROOM	A	900	2100	45	HM	MP	HM	MP		S	HW 27.0	M17/A-501	M17/A-501	I17/A-501	35		
D108	OFFICE	A	900	2100	45	HM	MP	HM	MP		-	HW 22.0	M17/A-501	M17/A-501	I7/A-501	25		
D109	TELECOM	A	900	2100	45	HM	MP	HM	MP		S	HW 25.0	M17/A-501	M17/A-501	I17/A-501	35		
D110	OFFICE	A	900	2100	45	HM	MP	HM	MP		-	HW 22.0	M17/A-501	M17/A-501	I7/A-501	25		
D111	CONFERENCE ROOM	A	900	2100	45	HM	MP	HM	MP		-	HW 22.0	M17/A-501	M17/A-501	I7/A-501	35		
D112	JANITOR	A	900	2100	45	HM	MP	HM	MP		-	HW 34.0	M17/A-501	M17/A-501	I17/A-501			
D113	WOMEN	A	900	2100	45	HM	MP	HM	MP		-	HW 40.0	M17/A-501	M17/A-501	E7/A-501			
D114	MEN	A	900	2100	45	HM	MP	HM	MP		-	HW 40.0	M17/A-501	M17/A-501	E7/A-501			
D115	BREAK ROOM	A	900	2100	45	HM	MP	HM	MP		-	HW 35.0	M17/A-501	M17/A-501	I17/A-501			
D116A	FORKLIFT CHARGE STATION	F	3000	3000	25	AL	MFR	AL	MFR		-	HW 1.0	E12/A-501	C17/A-501	A12/A-501			
D116B	FORKLIFT CHARGE STATION	A	900	2100	45	HM	MP	HM	MP									

	1	2	3	4	5	6	7	8	9	10	11	12	13	14	15	16	17	18	19	20	21
	WINDOW SCHEDULE - VMS (CLIN 0001)												WINDOW TYPES								
	WDW NO.	ROOM NAME	TYPE	SIZE		SILL HT	FRAME		GLAZING TYPE	DETAILS			REMARKS								
				W	HT		MAT	FIN		HEAD	JAMB	SILL									
	A112A	CONSOLIDATED BENCH REPAIR	B	2500	1200	900	AL	AF	GL-1	M1/A-504	I1/A-504	E1/A-504	1								
	A112B	CONSOLIDATED BENCH REPAIR	B	2500	1200	900	AL	AF	GL-1	M1/A-504	I1/A-504	E1/A-504	1								
	A202C	ADMIN & SHOP CONTROL	A	2400	1200	900	AL	AF	GL-1	M7/A-504	M7/A-504	A1/A-504									
	A202D	ADMIN & SHOP CONTROL	A	2400	1200	900	AL	AF	GL-1	M7/A-504	M7/A-504	A1/A-504									
	A202E	ADMIN & SHOP CONTROL	A	2400	1200	900	AL	AF	GL-1	M7/A-504	M7/A-504	A1/A-504									
	A202F	ADMIN & SHOP CONTROL	A	2400	1200	900	AL	AF	GL-1	M7/A-504	M7/A-504	A1/A-504									
	A205A	TRAINING ROOM	C	3200	1200	900	AL	AF	GL-1	M1/A-504	I1/A-504	E1/A-504	1								
	A205B	TRAINING ROOM	C	3000	1200	400	AL	AF	GL-1	M1/A-504	I1/A-504	E1/A-504	1								
	A205C	TRAINING ROOM	A	2400	1200	900	AL	AF	GL-1	M7/A-504	M7/A-504	A1/A-504									
	A205D	TRAINING ROOM	A	2400	1200	900	AL	AF	GL-1	M7/A-504	M7/A-504	A1/A-504									
	A205F	BREAK/ TRAINING/ CONFERENCE	B	2000	1200	400	AL	AF	GL-1	M1/A-504	I1/A-504	E1/A-504	1								
	A205G	BREAK/ TRAINING/ CONFERENCE	B	2000	1200	400	AL	AF	GL-1	M1/A-504	I1/A-504	E1/A-504	1								
	A206A	ADMIN & SHOP CONTROL OVERFLOW	B	1800	2100	0	AL	AF	GL-1	M1/A-504	I1/A-504	E1/A-504	1								
	A206C	ADMIN & SHOP CONTROL OVERFLOW	B	2000	1200	900	AL	AF	GL-1	M1/A-504	I1/A-504	E1/A-504	1								
	A206D	ADMIN & SHOP CONTROL OVERFLOW	B	2000	1200	900	AL	AF	GL-1	M1/A-504	I1/A-504	E1/A-504	1								
	A208	RECYCLING	B	2000	1200	900	AL	AF	GL-1	M1/A-504	I1/A-504	E1/A-504	1								
	A210	WOMEN	B	2000	1200	900	AL	AF	GL-1	M1/A-504	I1/A-504	E1/A-504	1, 2								
	A211	MEN	A	1200	1200	900	AL	AF	GL-1	M1/A-504	I1/A-504	E1/A-504	1, 2								
	A213	ELEV LOBBY	B	1800	2000	100	AL	AF	GL-1	M1/A-504	I1/A-504	E1/A-504	1								

WINDOW SCHEDULE - SSAW (CLIN 0004)													
WDW NO.	ROOM NAME	TYPE	SIZE		SILL HT	FRAME		GLAZING TYPE	DETAILS				REMARKS
			W	HT		MAT	FIN		HEAD	JAMB	SILL		
D102	CUSTOMER SERVICE AREA	A	1200	1200	900	AL	AF	GL-1	M1/A-504	I1/A-504	E1/A-504	1	
D103B	CLS OFFICE	A	1200	1200	900	AL	AF	GL-1	M1/A-504	I1/A-504	E1/A-504	1	
D103C	CLS OFFICE	A	1200	1200	900	AL	AF	GL-1	M1/A-504	I1/A-504	E1/A-504	1	
D103D	CLS OFFICE	A	1200	1200	900	AL	AF	GL-1	M1/A-504	I1/A-504	E1/A-504	1	
D104	OFFICE	A	1200	1200	900	AL	AF	GL-1	M1/A-504	I1/A-504	E1/A-504	1	
D105	STOCK CONTROL OFFICE	D	1200	900	900	AL	AF	GL-1	I7/A-504	E7/A-504	A5/A-504		
D106	OFFICE	A	1200	1200	900	AL	AF	GL-1	M1/A-504	I1/A-504	E1/A-504	1	
D108	OFFICE	A	1200	1200	900	AL	AF	GL-1	M1/A-504	I1/A-504	E1/A-504	1	
D110	OFFICE	A	1200	1200	900	AL	AF	GL-1	M1/A-504	I1/A-504	E1/A-504	1	
D114	MEN	D	1200	600	1550	AL	AF	GL-1	M1/A-504	I1/A-504	E1/A-504	1	
D115A	BREAK ROOM	B	2000	1200	950	AL	AF	GL-1	M1/A-504	I1/A-504	E1/A-504	1	
D115B	BREAK ROOM	B	2000	1200	950	AL	AF	GL-1	M1/A-504	I1/A-504	E1/A-504	1	

WINDOW SCHEDULE - COF SS (CLIN 0004)													
WDW NO.	ROOM NAME	TYPE	SIZE		SILL HT	FRAME		GLAZING TYPE	DETAILS			REMARKS	
			W	HT		MAT	FIN		HEAD	JAMB	SILL		
H112A	CLASSROOM	E	2400	900	1250	AL	AF	GL-1	I12/A-504	I12/A-504	E12/A-504	1	
H112B	CLASSROOM	E	2400	900	1250	AL	AF	GL-1	I12/A-504	I12/A-504	E12/A-504	1	
H113	OFFICE	E	2400	900	1250	AL	AF	GL-1	I12/A-504	I12/A-504	E12/A-504	1	
H122A	OPEN WORKSTA./ CONFERENCE	E	2400	900	1250	AL	AF	GL-1	I12/A-504	I12/A-504	E12/A-504	1	
H122B	OPEN WORKSTA./ CONFERENCE	E	2400	900	1250	AL	AF	GL-1	I12/A-504	I12/A-504	E12/A-504	1	
H125	XO OFFICE	E	2400	900	1250	AL	AF	GL-1	I12/A-504	I12/A-504	E12/A-504	1	
H132A	OPEN WORKSTA./ CONFERENCE	E	2400	900	1250	AL	AF	GL-1	I12/A-504	I12/A-504	E12/A-504	1	
H132B	OPEN WORKSTA./ CONFERENCE	E	2400	900	1250	AL	AF	GL-1	I12/A-504	I12/A-504	E12/A-504	1	
H135	XO OFFICE	E	2400	900	1250	AL	AF	GL-1	I12/A-504	I12/A-504	E12/A-504	1	
H212A	OPEN WORKSTA./ CONFERENCE	E	2400	900	1250	AL	AF	GL-1	I12/A-504	I12/A-504	G12/A-504	1	
H212B	OPEN WORKSTA./ CONFERENCE	E	2400	900	1250	AL	AF	GL-1	I12/A-504	I12/A-504	E12/A-504	1	
H215	XO OFFICE	E	2400	900	1250	AL	AF	GL-1	I12/A-504	I12/A-504	E12/A-504	1	
H222A	OPEN WORKSTA./ CONFERENCE	E	2400	900	1250	AL	AF	GL-1	I12/A-504	I12/A-504	E12/A-504	1	
H222B	OPEN WORKSTA./ CONFERENCE	E	2400	900	1250	AL	AF	GL-1	I12/A-504	I12/A-504	E12/A-504	1	
H225	XO OFFICE	E	2400	900	1250	AL	AF	GL-1	I12/A-504	I12/A-504	E12/A-504	1	
H232A	OPEN WORKSTA./ CONFERENCE	E	2400	900	1250	AL	AF	GL-1	I12/A-504	I12/A-504	G12/A-504	1	
H232B	OPEN WORKSTA./ CONFERENCE	E	2400	900	1250	AL	AF	GL-1	I12/A-504	I12/A-504	E12/A-504	1	
H235	XO OFFICE	E	2400	900	1250	AL	AF	GL-1	I12/A-504	I12/A-504	E12/A-504	1	

TRANSLUCENT WALL PANEL SCHEDULE - VMS (CLIN 0001)													
WDW NO.	ROOM NAME	TYPE	SIZE		SILL HT	FRAME		GLAZING TYPE	DETAILS			REMARKS	
			W	HT		MAT	FIN		HEAD	JAMB	SILL		
A101A	MACHINE SHOP/ WELDING AREA	TWP-1	7300	1200	6400	AL	AF	GL-2	L16/A-505	G16/A-505	B16/A-505		
A101B	REPAIR BAYS	TWP-1	7300	1200	6400	AL	AF	GL-2	L16/A-505	G16/A-505	B16/A-505		
A101C	REPAIR BAYS	TWP-1	7300	1200	6400	AL	AF	GL-2	L16/A-505	G16/A-505	B16/A-505		
A101D	REPAIR BAYS	TWP-1	7300	1200	6400	AL	AF	GL-2	L16/A-505	G16/A-505	B16/A-505		
A101E	REPAIR BAYS	TWP-1	7300	1200	6400	AL	AF	GL-2	L16/A-505	G16/A-505	B16/A-505		
A101F	REPAIR BAYS	TWP-1	7300	1200	6400	AL	AF	GL-2	L16/A-505	G16/A-505	B16/A-505		
A101G	REPAIR BAYS	TWP-1	7300	1200	6400	AL	AF	GL-2	L16/A-505	G16/A-505	B16/A-505		
A101H	GENERATOR MAINTENANCE	TWP-1	7300	1200	6400	AL	AF	GL-2	L16/A-505	G16/A-505	B16/A-505		
A101J	VEHICLE MAINTENANCE SHOP	TWP-1	7300	1200	6400	AL	AF	GL-2	L16/A-505	G16/A-505	B16/A-505		
A202A	ADMIN & SHOP CONTROL	TWP-1	6500	1200	900	AL	AF	GL-2	L16/A-505	G16/A-505	B16/A-505		
A206B	ADMIN & SHOP CONTROL OVERFLOW	TWP-1	4000	1200	400	AL	AF	GL-2	L16/A-505	G16/A-505	B16/A-505		

	1	2	3	4	5	6	7	8	9	10	11				
LOUVER SCHEDULE - VMS (CLIN 0001)															
LOUVER NO.	ROOM NAME	TYPE	LOUVER		SILL	FRAME		LOUVER		HOOD		DETAILS			REMARKS
			W	HT	HT	MAT	FIN	MAT	FIN	MAT	FIN	HEAD	JAMB	SILL	
A101I	MACHINE SHOP/ WELDING AREA	L2	3000	2500	8000	AL	AF	AL	AA	SSL	PT	G1/A-505	G1/A-505	A1/A-505	
A101K	REPAIR BAYS	L2	4750	2000	8600	AL	AF	AL	AA	SSL	PT	G1/A-505	G1/A-505	A1/A-505	
A107	MECHANICAL ROOM	L2	750	1100	3200	AL	AF	AL	AF	SSL	-	G1/A-505	G1/A-505	A1/A-505	
A108	MEN'S TOILET AND LOCKER ROOM	L2	1800	250	3350	AL	AF	AL	AF	SSL	-	G1/A-505	G1/A-505	A1/A-505	
A109	MACHINE SHOP/ WELDING AREA	L2	2000	1500	3600	AL	AF	AL	AA	SSL	PT	G1/A-505	G1/A-505	A1/A-505	
A111	NON SENSITIVE SECURE STORAGE	L2	500	500	4200	AL	AF	AL	AF	SSL	-	G1/A-505	G1/A-505	A1/A-505	
A112	CONSOLIDATED BENCH REPAIR	L2	250	200	4600	AL	AF	AL	AF	SSL	-	G1/A-505	G1/A-505	A1/A-505	
A115A	FLUID DISTRIBUTION ROOM	L2	400	300	4200	AL	AF	AL	AF	SSL	-	G1/A-505	G1/A-505	A1/A-505	
A115B	FLUID DISTRIBUTION ROOM	L2	750	900	3200	AL	AF	AL	AF	SSL	-	G1/A-505	G1/A-505	A1/A-505	
A121	HALL	L2	600	750	3200	AL	AF	AL	AF	SSL	-	G1/A-505	G1/A-505	A1/A-505	
A208	RECYCLING	L2	200	200	3250	AL	AF	AL	AF	SSL	-	G1/A-505	G1/A-505	A1/A-505	
A209A	BREAK/ TRAINING/ CONFERENCE	L2	300	450	3200	AL	AF	AL	AF	SSL	-	G1/A-505	G1/A-505	A1/A-505	
A209B	BREAK/ TRAINING/ CONFERENCE	L2	300	300	3200	AL	AF	AL	AF	SSL	-	G1/A-505	G1/A-505	A1/A-505	
A210	WOMEN	L2	300	200	3200	AL	AF	AL	AF	SSL	-	G1/A-505	G1/A-505	A1/A-505	
A211	MEN	L2	300	200	3200	AL	AF	AL	AF	SSL	-	G1/A-505	G1/A-505	A1/A-505	
LOUVER SCHEDULE - FP (CLIN 0001)															
LOUVER NO.	ROOM NAME	TYPE	LOUVER		SILL	FRAME		LOUVER		HOOD		DETAILS			REMARKS
			W	HT	HT	MAT	FIN	MAT	FIN	MAT	FIN	HEAD	JAMB	SILL	
F101A	FIRE PUMP	L2	550	400	300	AL	AF	AL	AA	SST	-	G1/A-505	G1/A-505	A1/A-505	
F101B	FIRE PUMP	L2	450	400	2900	AL	AF	AL	AA	SST	-	G1/A-505	G1/A-505	A1/A-505	
LOUVER SCHEDULE - CH (CLIN 0001)															
LOUVER NO.	ROOM NAME	TYPE	LOUVER		SILL	FRAME		LOUVER		HOOD		DETAILS			REMARKS
			W	HT	HT	MAT	FIN	MAT	FIN	MAT	FIN	HEAD	JAMB	SILL	
G101	UTILITY	L2	350	350	3000	AL	AF	AL	AA	SST	-	G1/A-505	G1/A-505	A1/A-505	
LOUVER SCHEDULE - OS (CLIN 0002)															
LOUVER NO.	ROOM NAME	TYPE	LOUVER		SILL	FRAME		LOUVER		HOOD		DETAILS			REMARKS
			W	HT	HT	MAT	FIN	MAT	FIN	MAT	FIN	HEAD	JAMB	SILL	
B101A	ALPHA STORAGE	L3	900	700	2150	AL	AF	AL	AA	SST	-	L12/A-505	L12/A-505		
B101B	ALPHA STORAGE	L2	700	700	2250	AL	AF	AL	AA	SST	-	G1/A-505	G1/A-505	A1/A-505	
B101C	ALPHA CLOSET	L2	350	350	2600	AL	AF	AL	AA	SST	-	G1/A-505	G1/A-505	A1/A-505	
B102A	BRAVO STORAGE	L3	900	700	2150	AL	AF	AL	AA	SST	-	L12/A-505	L12/A-505		
B102B	BRAVO STORAGE	L2	700	700	2250	AL	AF	AL	AA	SST	-	G1/A-505	G1/A-505	A1/A-505	
B102C	BRAVO CLOSET	L2	350	350	2600	AL	AF	AL	AA	SST	-	G1/A-505	G1/A-505	A1/A-505	
B103A	CHARLIE STORAGE	L3	900	700	2150	AL	AF	AL	AA	SST	-	L12/A-505	L12/A-505		
B103B	CHARLIE STORAGE	L2	700	700	2250	AL	AF	AL	AA	SST	-	G1/A-505	G1/A-505	A1/A-505	
B103C	CHARLIE CLOSET	L2	350	350	2600	AL	AF	AL	AA	SST	-	G1/A-505	G1/A-505	A1/A-505	
B104A	DELTA STORAGE	L3	900	700	2150	AL	AF	AL	AA	SST	-	L12/A-505	L12/A-505		
B104B	DELTA STORAGE	L2	700	700	2250	AL	AF	AL	AA	SST	-	G1/A-505	G1/A-505	A1/A-505	
B104C	DELTA CLOSET	L2	350	350	2600	AL	AF	AL	AA	SST	-	G1/A-505	G1/A-505	A1/A-505	
B105A	ECHO STORAGE	L3	900	700	2150	AL	AF	AL	AA	SST	-	L12/A-505	L12/A-505		
B105B	ECHO STORAGE	L2	700	700	2250	AL	AF	AL	AA	SST	-	G1/A-505	G1/A-505	A1/A-505	
B105C	ECHO CLOSET	L2	350	350	2600	AL	AF	AL	AA	SST	-	G1/A-505	G1/A-505	A1/A-505	
B106A	HQ STORAGE	L3	900	700	2150	AL	AF	AL	AA	SST	-	L12/A-505	L12/A-505		
B106B	HQ STORAGE	L2	700	700	2250	AL	AF	AL	AA	SST	-	G1/A-505	G1/A-505	A1/A-505	
B106C	HQ CLOSET	L2	350	350	2600	AL	AF	AL	AA	SST	-	G1/A-505	G1/A-505	A1/A-505	
LOUVER SCHEDULE - POL & HAZMAT (CLIN 0002)															
LOUVER NO.	ROOM NAME	TYPE	LOUVER		SILL	FRAME		LOUVER		HOOD		DETAILS			REMARKS
			W	HT	HT	MAT	FIN	MAT	FIN	MAT	FIN	HEAD	JAMB	SILL	
C102A	HAZMAT STORAGE	L2	750	700	1900	AL	AF	AL	AA	SST	-	G1/A-505	G1/A-505	A1/A-505	
C102B	POL STORAGE	L2	750	700	1900	AL	AF	AL	AA	SST	-	G1/A-505	G1/A-505	A1/A-505	
C102C	POL STORAGE	L2	1100	700	300	AL	AF	AL	AA	SST	-	G1/A-505	G1/A-505	A1/A-505	
C102D	POL STORAGE	L2	1100	700	300	AL	AF	AL	AA	SST	-	G1/A-505	G1/A-505	A1/A-505	
LOUVER SCHEDULE - SSAW (CLIN 0004)															
LOUVER NO.	ROOM NAME	TYPE	LOUVER		SILL	FRAME		LOUVER		HOOD		DETAILS			REMARKS
			W	HT	HT	MAT	FIN	MAT	FIN	MAT	FIN	HEAD	JAMB	SILL	
D114C	MEN	L2	300	300	4300	AL	AF	AL	AF	SSL	-	G1/A-505	G1/A-505	A1/A-505	
D116	FORKLIFT CHARGE STATION	L2	450	450	3750	AL	AF	AL	AF	SSL	-	G1/A-505	G1/A-505	A1/A-505	
D118B	WAREHOUSE	L2	2150	1250	4350	AL	AF	AL	AF	SSL	-	G1/A-505	G1/A-505	A1/A-505	
D118C	WAREHOUSE	L2	2150	1250	4350	AL	AF	AL	AF	SSL	-	G1/A-505	G1/A-505	A1/A-505	
D120	CUSTOMER ISSUE BAY	L2	1250	950	3850	AL	AF	AL	AF	SSL	-	G1/A-505	G1/A-505	A1/A-505	
D121A	RECEIVING/ISSUE BAY	L2	4100	1300	3650	AL	AF	AL	AA	SSL	-	G1/A-505	G1/A-505	A1/A-505	
D121B	RECEIVING/ISSUE BAY	L2	4100	1300	3650	AL	AF	AL	AA	SSL	-	G1/A-505	G1/A-505	A1/A-505	
D125	MECHANICAL ROOM	L2	900	750	2950	AL	AF	AL	AF	SSL	-	G1/A-505	G1/A-505	A1/A-505	
D125A	MECHANICAL ROOM	L2	300	200	3000	AL	AF	AL	AF	SSL	-	G1/A-505	G1/A-505	A1/A-505	
D128	ENTRY	L2	450	300	4000	AL	AF	AL	AF	SSL	-	G1/A-505	G1/A-505	A1/A-505	
D129	MEN	L2	450	450	4150	AL	AF	AL	AF	SSL	-	G1/A-505	G1/A-505	A1/A-505	
D131	MEN	L2	450	450	3950	AL	AF	AL	AF	SSL	-	G1/A-505	G1/A-505	A1/A-505	
D132	WAREHOUSE	L2	2800	1250	3600	AL	AF	AL	AF	SSL	-	G1/A-505	G1/A-505	A1/A-505	
LOUVER SCHEDULE - COF SS (CLIN 0004)															
LOUVER NO.	ROOM NAME	TYPE	LOUVER		SILL	FRAME		LOUVER		HOOD		DETAILS			REMARKS
			W	HT	HT	MAT	FIN	MAT	FIN	MAT	FIN	HEAD	JAMB	SILL	
H102	MEN'S TOILET	L2	450	305	3000	AL	AF	AL	AF	SSL	SST	L9/ A-505	L9/ A-505	A8/ A-505	
H103	WOMEN'S TOILET	L2	450	305	3000	AL	AF	AL	AF	SSL	SST	L9/ A-505	L9/ A-505	A8/ A-505	
H111	STORAGE	L2	450	305	3000	AL	AF	AL	AF	SSL	SST	L9/ A-505	L9/ A-505	A8/ A-505	
H126	STOR	L2	450	305	3000	AL	AF	AL	AF	SSL	SST	L9/ A-505	L9/ A-505	A8/ A-505	
H136	STOR	L2	450	305	3000	AL	AF	AL	AF	SSL	SST	L9/ A-505	L9/ A-505	A8/ A-505	
H202	MEN'S TOILET	L2	450	305	2750	AL	AF	AL	AF	SSL	SST	L9/ A-505	L9/ A-505	A8/ A-505	
H203	WOMEN'S TOILET	L2	450	305	2750	AL	AF	AL	AF	SSL	SST	L9/ A-505	L9/ A-505	A8/ A-505	
H216	STOR	L2	450	305	2450	AL	AF	AL	AF	SSL	SST	L9/ A-505	L9/ A-505	A8/ A-505	
H226	STOR	L2	450	305	2450	AL	AF	AL	AF	SSL	SST	L9/ A-505	L9/ A-505	A8/ A-505	
H236	STOR	L2	450	305	2450	AL	AF	AL	AF	SSL	SST	L9/ A-505	L9/ A-505	A8/ A-505	

1	2	3	4	5	6	7	8	9	10	11	12	13	14	15	16	17	18	19	20	21		
MATERIAL FINISH SCHEDULE																						
MATERIAL TYPE		DESCRIPTION				MANUFACTURER / SUPPLIER				PATTERN / TYPE				COLOR/ MODEL				SIZE		REMARK		
ACOUSTICAL CEILING TILE: ACT-																						
ACT-1		ACOUSTICAL CEILING TILE				DAIKEN				TRAVERTINE				TK5512-1B				600 X 1200		PER ROOM FINISH SCHEDULE		
CERAMIC TILE: CT-																						
CT-1		CERAMIC TILE				LIXIL CORPORATION				FOG BORDER				DTL-2330P1/FGB-4				227 X 27		KITCHEN BACKSPLASH		
CT-1A		CERAMIC TILE				NAGOYA MOZAIC				LUMEN				LUM-04				28 X 28		KITCHEN BACKSPLASH		
CT-2		CERAMIC TILE				NAGOYA MOZAIC				WET AREA				WET-150-110				150 X 150		MEN'S SHOWER FLOOR		
CT-2A		CERAMIC TILE				NAGOYA MOZAIC				WET AREA				WET-150-108				150 X 150		MEN'S SHOWER FLOOR		
CT-3		CERAMIC TILE				NAGOYA MOZAIC				WET AREA				WET-150-109				150 X 150		WOMEN'S SHOWER FLOOR		
CT-3A		CERAMIC TILE				NAGOYA MOZAIC				WET AREA				WET-150-101				150 X 150		WOMEN'S SHOWER FLOOR		
CORNER GUARD: CG-																						
CG-1		VINYL CORNER GUARD				INPRO CORPORATION				160 HIGH IMPACT CORNER GUARD				0106 - DOVE GRAY				SEE DETAILS				
CG-2		STAINLESS STEEL CORNER GUARD				INPRO CORPORATION				183124H-430				430 STAINLESS STEEL, 16 GAUGE				SEE DETAILS				
FUEL RESISTIVE RESINOUS FLOORING: FRRF-																						
FRRF-1		FUEL RESISTIVE RESINOUS FLOORING				-				-				-				-		MAINTENANCE AREA FLOOR		
STATIC-CONTROL RESILIENT FLOORING: SCRF-																						
SCRF-1		STATIC-CONTROL RESILIENT FLOORING																		TELECOM, COMM & SIPRNET ROOMS		
LOCKER: LKR-																						
LKR-1		METAL LOCKER, DOUBLE TIER				SEIKOFAMILY				SLK LOCKER				NEWGREY				300 X 515 X 1800		LOCKER ROOMS		
LKR-1A		METAL LOCKER, DOUBLE TIER				SEIKOFAMILY				SLB LOCKER				WALNUT				300 X 515 X 1800		LOCKER ROOMS		
PAINT: PT-																						
PT-1		FIELD PAINT				JPMA STANDARD PAINT COLORS				-				22-90B				-		WALLS AND CEILINGS		
PT-1A		FIELD PAINT				JPMA STANDARD PAINT COLORS				-				25-90A				-		WALLS AND CEILINGS		
PT-2		ACCENT PAINT				JPMA STANDARD PAINT COLORS				-				35-70B				-		ACCENT		
PT-2A		ACCENT PAINT				JPMA STANDARD PAINT COLORS				-				69-50A				-		ACCENT		
PT-3		DOOR AND FRAME PAINT				JPMA STANDARD PAINT COLORS				-				22-80B				-		DOORS AND FRAMES		
PT-3A		DOOR AND FRAME PAINT				JPMA STANDARD PAINT COLORS				-				22-75A				-		DOORS AND FRAMES		
PLASTIC LAMINATE: PLAM-																						
PLAM-1		PLASTIC LAMINATE				AICA				CERARL				FJ-695ZJN67				SEE DETAILS		ALL CASEWORK		
PLAM-1A		PLASTIC LAMINATE				AICA				CELSUS				TNY10199K				SEE DETAILS		ALL CASEWORK		
PORCELAIN TILE: PORC-																						
PORC-1		PORCELAIN FLOOR TILE				LIXIL				KILAMIC				IPF-300/RSL-23W				300 X 300		MEN'S TOILET - FLOOR		
PORC-1A		PORCELAIN FLOOR TILE				NAGOYA MOSAIC				PIETRA SOGNI				PAN-X8130G				600 X 300		MEN'S TOILET - FLOOR		
PORC-2		PORCELAIN FLOOR TILE				LIXIL				KILAMIC				IPF-300/RSL-22W				300 X 300		WOMEN'S TOILET - FLOOR		
PORC-2A		PORCELAIN FLOOR TILE				NAGOYA MOSAIC				PIETRA SOGNI				PAN-X8120G				600 X 300		WOMEN'S TOILET - FLOOR		
PORC-3		PORCELAIN FLOOR TILE				LIXIL				SHINSAGAN TILE □				NSA-150N/18				150 X 150		MEN'S TOILET - WALL		
PORC-3A		PORCELAIN FLOOR TILE				NAGOYA MOSAIC				PIETRA SOGNI				PAN-L8230G				200 X 200		MEN'S TOILET - WALL		
PORC-4		PORCELAIN FLOOR TILE				LIXIL				SHINSAGAN TILE □				NSA-150N/15				150 X 150		WOMEN'S TOILET - WALL		
PORC-4A		PORCELAIN FLOOR TILE				NAGOYA MOSAIC				PIETRA SOGNI				PAN-L8220G				200 X 200		WOMEN'S TOILET - WALL		
RECESSED ENTRY MAT: REM-																						
REM-1		RECESSED ENTRY MAT SYSTEM				MIZUSHIMA				CLIK-19				GREY				SEE PLANS		MAIN ENTRY		
RUBBER COVE BASE: RCB-																						
RCB-1		RUBBER COVE BASE				TOLI				SOFT				TH100RN25				100		PER ROOM FINISH SCHEDULE		
RCB-1A		RUBBER COVE BASE				TOLI				SOFT				TH100RN35				100		PER ROOM FINISH SCHEDULE		
RCB-2		RUBBER COVE BASE				TOLI				SOFT				TH100RN31				100		SIMULATOR ROOMS		
SOLID SURFACE: SS-																						
SS-1		SOLID SURFACE				CORIAN				-				SICCUI BEIGE				SEE PLANS		ALL CASEWORK		
SS-1A		SOLID SURFACE				CORIAN				-				EVEREST				SEE PLANS		ALL CASEWORK		
TOILET PARTITION PANEL: TPTN-																						
TPTN-1		TOILET PARTITION				AICA				AICARABIAN				SHIPPOU SHIRONEZU				SEE PLANS		RESTROOMS		
TPTN-2		TOILET PARTITION				AICA				CERARL				LINEA CERVEJANTE/PALE				SEE PLANS		RESTROOMS		
VINYL COMPOSITE TILE: VCT-																						
VCT-1		VINYL COMPOSITE TILE				TOLI				MOKURIN				MOT2017				100 X 900		HALLWAYS, ENTRY		
VCT-1A		VINYL COMPOSITE TILE				TOLI				GRANOBLE				GNT7511				450 X 450		HALLWAYS, ENTRY		
VCT-2		VINYL COMPOSITE TILE				TOLI				REFRIPE				RFT7007				450 X 450		OFFICES		
VCT-2A		VINYL COMPOSITE TILE				TOLI				REFRIPE				RFT7008				450 X 450		OFFICES		
WINDOW ROLLER SHADE: WS-																						
WS-1		WINDOW ROLLERSHADE (PRIVACY)				TOSO				KONPLE05				GREY/TR-6280				SEE PLANS		PER WINDOW SCHEDULE		
WS-1A		WINDOW ROLLERSHADE (PRIVACY)				TOSO				KONPLE05				BEIGE/TR-6279				SEE PLANS		PER WINDOW SCHEDULE		

1

2

3

4

5

6

7

8

9

10

11

12

13

14

15

16

17

18

19

20

21

P

O

N

M

L

K

J

I

H

G

F

E

D

C

B

A

TERMINATE
GWB AND
FINISH 150
ABOVE
CEILING

AIR SPACE,
SEE PLANS
FOR DIM

CEILING AS SCHED
WHERE OCCURS

50 METAL STUDS
@ 303 O.C.

1 LAYER 15 THK GWB

50 BOTTOM RUNNER

BASE AS SCHEDULED
CONT BEAD OF NON-
HARDENING CAULKING
FLR FIN AS SCHED

70

303

303

70

303

303

TYPE	DESCRIPTION	GWB/FIN HEIGHT	CURB	INSUL	STC
9	65 STUD	TO STRUCT	NO	YES	STC 45 (RW44)
9A	65 STUD, NO AIR SPACE	TO STRUCT	NO	YES	-
9B	65 STUD, NO INSULATION	TO STRUCT	NO	NO	-
9C	100 STUD, NO INSULATION	TO STRUCT	NO	NO	-
9D	19 THK PLYWD BACKERBOARD OVER 65 STUD, R-5.7 INSUL BTWN STUD FRMG AND CONC WALL	TO STRUCT	NO	YES	STC 45 (RW44)

CEILING AS SCHED.
WHERE OCCURS

R-6.5 CONTINUOUS
RIGID INSULATION

15 GWB W/
FIN AS SCHED

BASE AS
SCHEDULED

FLR FIN AS SCHED

R-13 BATT INSUL

HSS WO. SEE
STRUCT DWGS

SELF-ADHERING
UNDERLAYMENT ON
25 THK PLYWD
SHEATHING

ALUM SIDING

CONC CURB

100

100

TYPE	DESCRIPTION	GWB/FIN HEIGHT	CURB	INSUL	STC
E1	15 GWB OVER 50 MTL STUD FRMG, R-6.5 CI RIGID INSUL, R-13 BATT INSUL BTWN HSS FRMG, ALUM SIDING ON SELF-ADHERING UNDERLAYMENT ON 25 THK PLYWD SHEATHING	TO STRUCT	YES	YES	-

US Army Corps
of Engineers ®

ISSUE DATE:

SOLICITATION NO.:

CONTRACT NO.:

W912N7-17-D-0003

DESIGNED BY:
KELINGWOOD

DRAWN BY:
TROYLO, J. MANUJA

CHECKED BY:

SUBMITTED BY:

SIZE:
ANSI D

US ARMY CORPS OF ENGINEERS
JAPAN ENGINEER DISTRICT
OKINAWA AREA OFFICE
APO AP 96376-5132

DESIGN PARTNERS INCORPORATED
1580 MAKALOA STREET, SUITE 1100
HONOLULU, HAWAII 96814

APO AP 96343-5010
FY20 MCA PN77833 VEHICLE MAINTENANCE SHOP

PARTITION TYPES

SHEET ID

A-632

DATE

DESCRIPTION

MARK

File Path:

12/17/2025 5:18:30 AM

Plot Date:

Autodesk Docs/SPN/JED DC VEHICLE MAINTENANCE SHOP/511795_TENAF_ARCH_V0221.dwg

INTERMEDIATE DESIGN

1	2	3	4	5	6	7	8	9	10	11	12	13	14	15	16	17	18	19	20	21
SIGNAGE SCHEDULE - COF SS (CLIN 0004)											SIGNAGE SCHEDULE - SSAW (CLIN 0004)									
ROOM NO.	ROOM NAME	DOOR NUMBER (LOCATION)	SIGNAGE NUMBER	MOUNTING TYPE	SIGN TYPE	QUANTITY	SIGN COPY ROOM NAME	SIGN COPY ROOM NUMBER	REMARKS	ROOM NO.	ROOM NAME	DOOR NUMBER (LOCATION)	SIGNAGE NUMBER	MOUNTING TYPE	SIGN TYPE	QUANTITY	SIGN COPY ROOM NAME	SIGN COPY ROOM NUMBER	REMARKS	
H100	MECHANICAL YARD	H100	H100	2	F	1	MECHANICAL YARD	H100		D101	ENTRY	D101A	D101A	1	A	1	ENTRY			
H101	HALL	H101	H101A	1	A	1	HALL			D101	ENTRY	D101B	D101B	1	F	1	EXIT			
H101	HALL	H101	H101B	1	F	1	EXIT			D101	ENTRY	D101B	D101C	1	K	1	FIRE EXTINGUISHER			
H102	MEN'S TOILET	H102	H102	1	D	1	MEN			D103	MEN	D103	D103	1	B	1	CLS OFFICE	D101		
H103	WOMEN'S TOILET	H103	H103	1	C	1	WOMEN			D104	OFFICE	D104	D104	1	B	1	OFFICE	D102		
H104	JANITOR	H104	H104	1	A	1	JANITOR			D105	STOCK CONTROL OFFICE	D105	D105	1	A	1	STOCK CONTROL OFFICE	D103		
H105	TELECOM	H105	H105	2	A	1	TELECOM			D106	OFFICE	D106	D106	1	B	1	OFFICE	D104		
H106	ELEC	H106	H106A	2	A	1	ELEC			D107	SIPR ROOM	D107	D107	1	A	1	SIPR ROOM			
H110	VEST	H110	H110A	2	A	1	VEST			D108	OFFICE	D108	D108	1	B	1	OFFICE	D105		
H110	VEST	H110	H110B	2	F	1	EXIT			D109	TELECOM	D109	D109	1	A	1	TELECOM			
H110	VEST	H110	H110C	6	K	1	FIRE EXTINGUISHER			D110	OFFICE	D110	D110	1	B	1	OFFICE	D106		
H111	STORAGE	H111	H111	2	A	1	STORAGE	H102A		D111	CONFERENCE ROOM	D111	D111	1	A	1	CONFERENCE ROOM	D107		
H112	VEST	H112	H112	2	A	1	VEST	H102		D112	JANITOR	D112	D112	3	A	1	JANITOR			
H113	STORAGE	H113	H113	2	A	1	OFFICE	H101		D113	WOMEN	D113	D113	1	C	1	WOMEN			
H120	ENTRY	H120	H120A	2	A	1	HEADQUARTERS BATTERY	H103		D114	MEN	D114	D114	1	D	1	MEN			
H120	ENTRY	H120	H120B	2	F	1	EXIT			D115	BREAK ROOM	D115	D115	1	A	1	BREAK ROOM	D108		
H120	ENTRY	H120	H120C	6	K	1	FIRE EXTINGUISHER			D116	FORKFLIFT CHARGE STATION	D116A	D116	1	A	1	FORKFLIFT CHARGE STATION	D109		
H123	CO OFFICE	H123	H123	1	B	1	CO OFFICE	H103A		D117	SECURE STORAGE	D117	D117	2	A	1	SECURE STORAGE	D110		
H124	1ST SGT OFFICE	H124	H124	1	B	1	1ST SGT OFFICE	H103B		D118	WAREHOUSE	D118A	D118A	1	A	1	WAREHOUSE	D113A		
H125	XO OFFICE	H125	H125	1	B	1	XO OFFICE	H103C		D118	WAREHOUSE	D118A	D118B	1	F	1	EXIT			
H126	STORAGE	H126	H126	1	A	1	STORAGE			D118	WAREHOUSE	D118A	D118C	6	K	1	FIRE EXTINGUISHER			
H127	COMM	H127	H127	1	A	1	COMM			D118	WAREHOUSE	D118D	D118E	1	F	1	EXIT			
H130	ENTRY	H130	H130A	2	A	1	ALPHA BATTERY	H104		D118	WAREHOUSE	D118D	D118F	6	K	1	FIRE EXTINGUISHER			
H130	ENTRY	H130	H130B	2	F	1	EXIT			D118	WAREHOUSE	D118D	D118D	1	A	1	WAREHOUSE	D113B		
H130	ENTRY	H130	H130C	6	K	1	FIRE EXTINGUISHER			D120	CUSTOMER ISSUE BAY	D120B	D120B	2	A	1	CUSTOMER ISSUE BAY			
H133	CO OFFICE	H133	H133	1	B	1	CO OFFICE	H104A		D120	CUSTOMER ISSUE BAY	D120A	D120A	2	A	1	CUSTOMER ISSUE BAY	D112		
H134	1ST SGT OFFICE	H134	H134	1	B	1	1ST SGT OFFICE	H104B		D120	CUSTOMER ISSUE BAY	D120B	D120E	2	A	1	CUSTOMER ISSUE BAY			
H135	XO OFFICE	H135	H135	1	B	1	XO OFFICE	H104C		D120	CUSTOMER ISSUE BAY	D120A	D120C	2	F	1	EXIT			
H136	STORAGE	H136	H136	1	A	1	STORAGE			D120	CUSTOMER ISSUE BAY	D120A	D120D	6	K	1	FIRE EXTINGUISHER			
H137	COMM	H137	H137	1	A	1	COMM			D122	TURN-IN BAY	D122	D122A	2	A	1	TURN-IN BAY	D113C		
H201	HALL	H201	H201A	1	A	1	HALL			D122	TURN-IN BAY	D122	D122B	2	F	1	EXIT			
H201	HALL	H201	H201B	1	F	1	EXIT			D122	TURN-IN BAY	D122	D122C	6	K	1	FIRE EXTINGUISHER			
H201	HALL	-	H201C	6	K	1	FIRE EXTINGUISHER			D123	CORRIDOR	D123	D123	1	A	1	CORRIDOR			
H202	MEN'S TOILET	H202	H202	1	D	1	MEN			D124	ELECTRICAL ROOM	D124	D124	1	A	1	ELECTRICAL ROOM			
H203	WOMEN'S TOILET	H203	H203	1	C	1	WOMEN			D125	MECHANICAL ROOM	D125	D125	1	A	1	MECHANICAL ROOM			
H204	JANITOR	H204	H204	1	A	1	JANITOR			D126	SECURE STORAGE	D126	D126	2	A	1	SECURE STORAGE	D114		
H205	TELECOM	H205	H205	2	A	1	TELECOM			D127	MECHANICAL YARD	D127	D127	2	A	1	MECHANICAL YARD			
H210	ENTRY	H210	H210A	2	A	1	BRAVO BATTERY	H105		D128	ENTRY	D128A	D128A	1	A	1	ENTRY			
H210	ENTRY	H210	H210B	2	F	1	EXIT			D128	ENTRY	D128B	D128B	1	F	1	EXIT			
H210	VEST	H210	H210C	6	K	1	FIRE EXTINGUISHER			D129	CORRIDOR	D129A	D129A	3	A	1	CORRIDOR			
H213	CO OFFICE	H213	H213	1	B	1	CO OFFICE	H105A		D129	CORRIDOR	D129B	D129B	3	A	1	CORRIDOR			
H214	1ST SGT OFFICE	H214	H214	1	B	1	1ST SGT OFFICE	H105B		D129	CORRIDOR	D129A	D129C	3	A	1	CORRIDOR			
H215	XO OFFICE	H215	H215	1	B	1	XO OFFICE	H105C		D130	FIRE/RISER PUMP	D130	D130	2	A	1	FIRE/RISER PUMP			
H216	STOR	H216	H216	1	A	1	STORAGE													
H217	COMM	H217	H217	1	A	1	COMM													
H220	ENTRY	H220	H220A	2	A	1	CHARLIE BATTERY	H106												
H220	ENTRY	H220	H220B	2	F	1	EXIT			ROOM NO.	ROOM NAME	DOOR NUMBER (LOCATION)	SIGNAGE NUMBER	MOUNTING TYPE	SIGN TYPE	QUANTITY	SIGN COPY ROOM NAME	SIGN COPY ROOM NUMBER	REMARKS	
H220	ENTRY	H220	H220C	6	K	1	FIRE EXTINGUISHER			E101	UNSERVICEABLE BULK STORAGE	-	E101B	6	K	1	UNSERVICEABLE BULK STORAGE			
H223	CO OFFICE	H223	H223	1	B	1	CO OFFICE	H106A		E101	UNSERVICEABLE BULK STORAGE	E101	E101A	2	A	1	UNSERVICEABLE BULK STORAGE	E101		
H224	1ST SGT OFFICE	H224	H224	1	B	1	1ST SGT OFFICE	H106B		E101	UNSERVICEABLE BULK STORAGE	E101	E101A	2	A	1	UNSERVICEABLE BULK STORAGE	E101		
H225	XO OFFICE	H225	H225	1	B	1	XO OFFICE	H106C		E102	SERVICEABLE BULK STORAGE	E102	E102A	1	A	1	SERVICEABLE BULK STORAGE	E102		
H226	STOR	H226	H226	1	A	1	STORAGE			E102	SERVICEABLE BULK STORAGE	-	E102B	6	K	1	SERVICEABLE BULK STORAGE			
H227	COMM	H227	H227	1	A	1	COMM													
H230	ENTRY	H230	H230A	2	A	1	DELTA BATTERY	H107												
H230	ENTRY	H230	H230B	2	F	1	EXIT													
H230	ENTRY	H230	H230C	6	K	1	FIRE EXTINGUISHER													
H233	CO OFFICE	H233	H233	1	B	1	CO OFFICE	H107A												
H234	1ST SGT OFFICE	H234	H234	1	B	1	1ST SGT OFFICE	H107B												
H235	XO OFFICE	H235	H235	1	B	1	XO OFFICE	H107C												
H236	STOR	H236	H236	1	A	1	STORAGE													
H237	COMM	H237	H237	1	A	1	COMM													

[illegible]

Autodesk Docs://SSFM JED IDC VEHICLE MAINTENANCE SHOP/511758 TEMF ARCH v2022.rvt

File Path:

Plot Date: 12/17/2025 5:18:40 AM

INTERMEDIATE DESIGN

GENERAL NOTES


1. REFER TO A-551 FOR SIGNAGE TYPES, MOUNTING TYPES AND NOTES.
2. REFER TO SHEET A-D151, A-E151 AND A-H151 FOR SIGNAGE PLANS.

SHEET ID

A-652



B1 RAILING TRANSITION AT LANDING

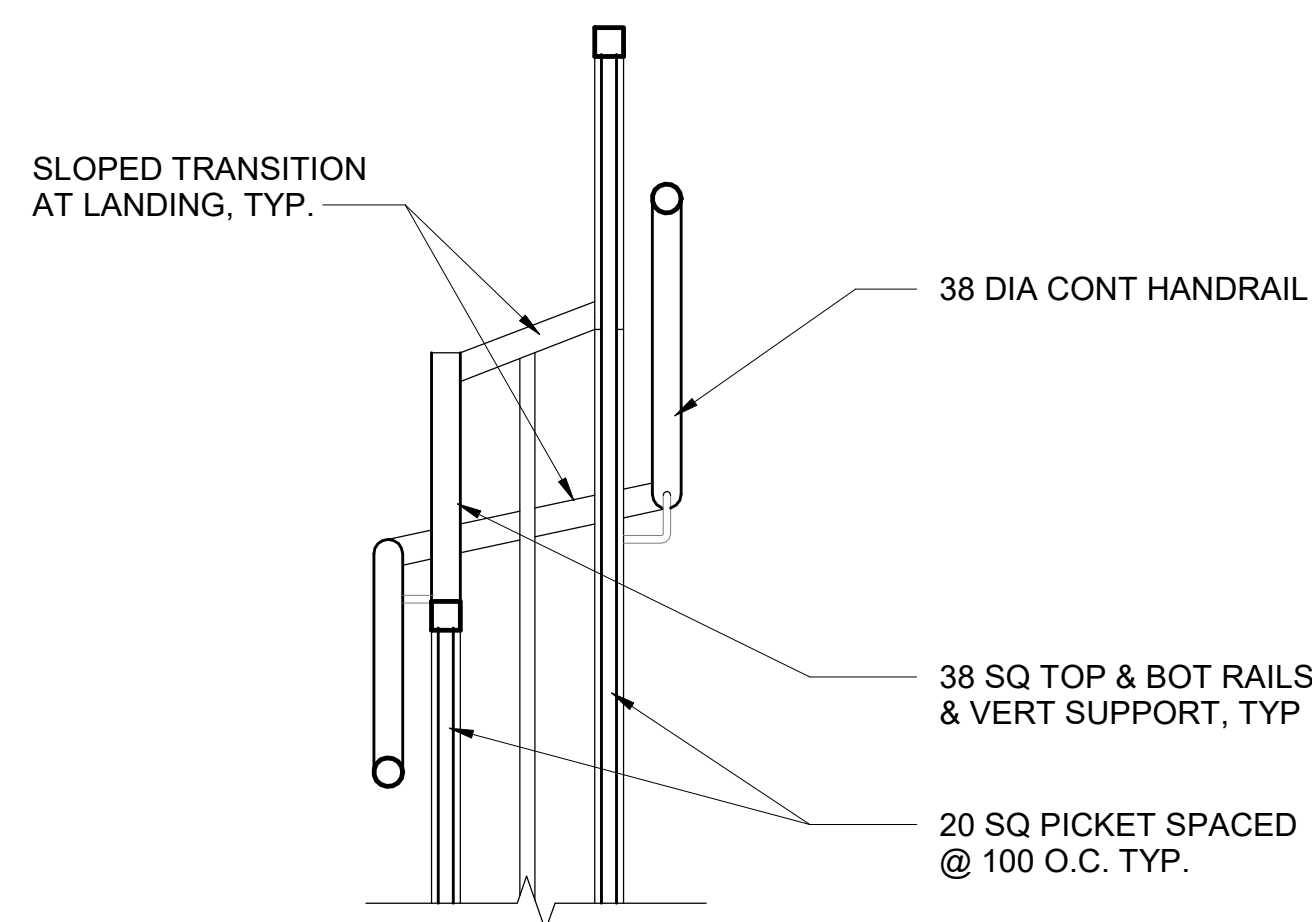[illegible]


DESIGNED BY: J. J. WOOD	ISSUE DATE:
DRAWN BY: IROLLO J. MANUIA	SOLICITATION NO.:
CHECKED BY: D. MONTANO	CONTRACT NO.:
DATE:	W972KN-17-J-0003
SUBMITTED BY:	
SIZE:	

APO AP 96343-5010
FY20 MCA PN77833 VEHICLE MAINTENANCE SHOP


STAIR RAILING DETAILS

SHEET ID


A-752

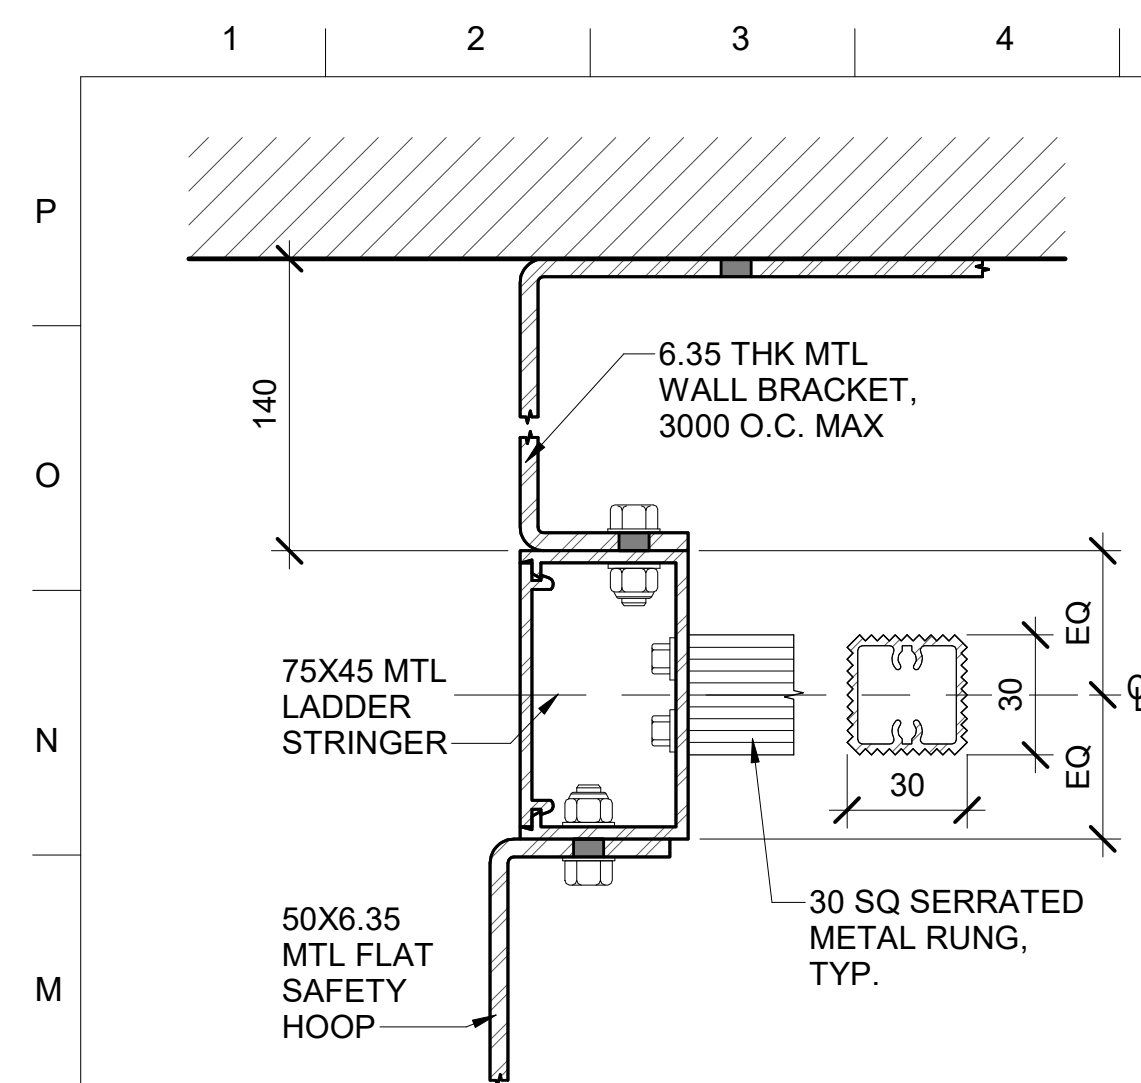


L1 CAGE LADDER TREAD

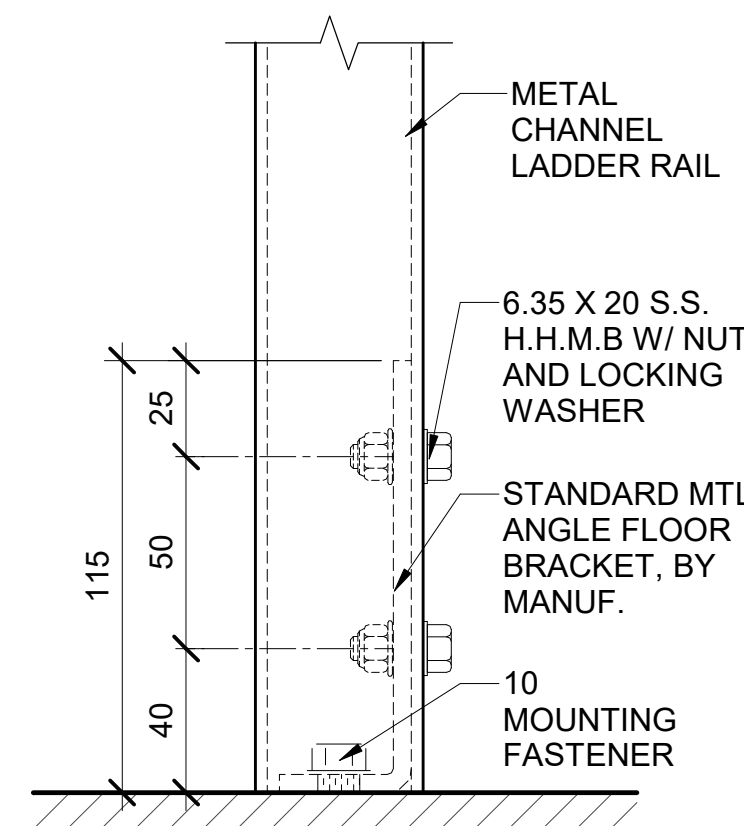


L8 FLOOR MOUNT BRACKET

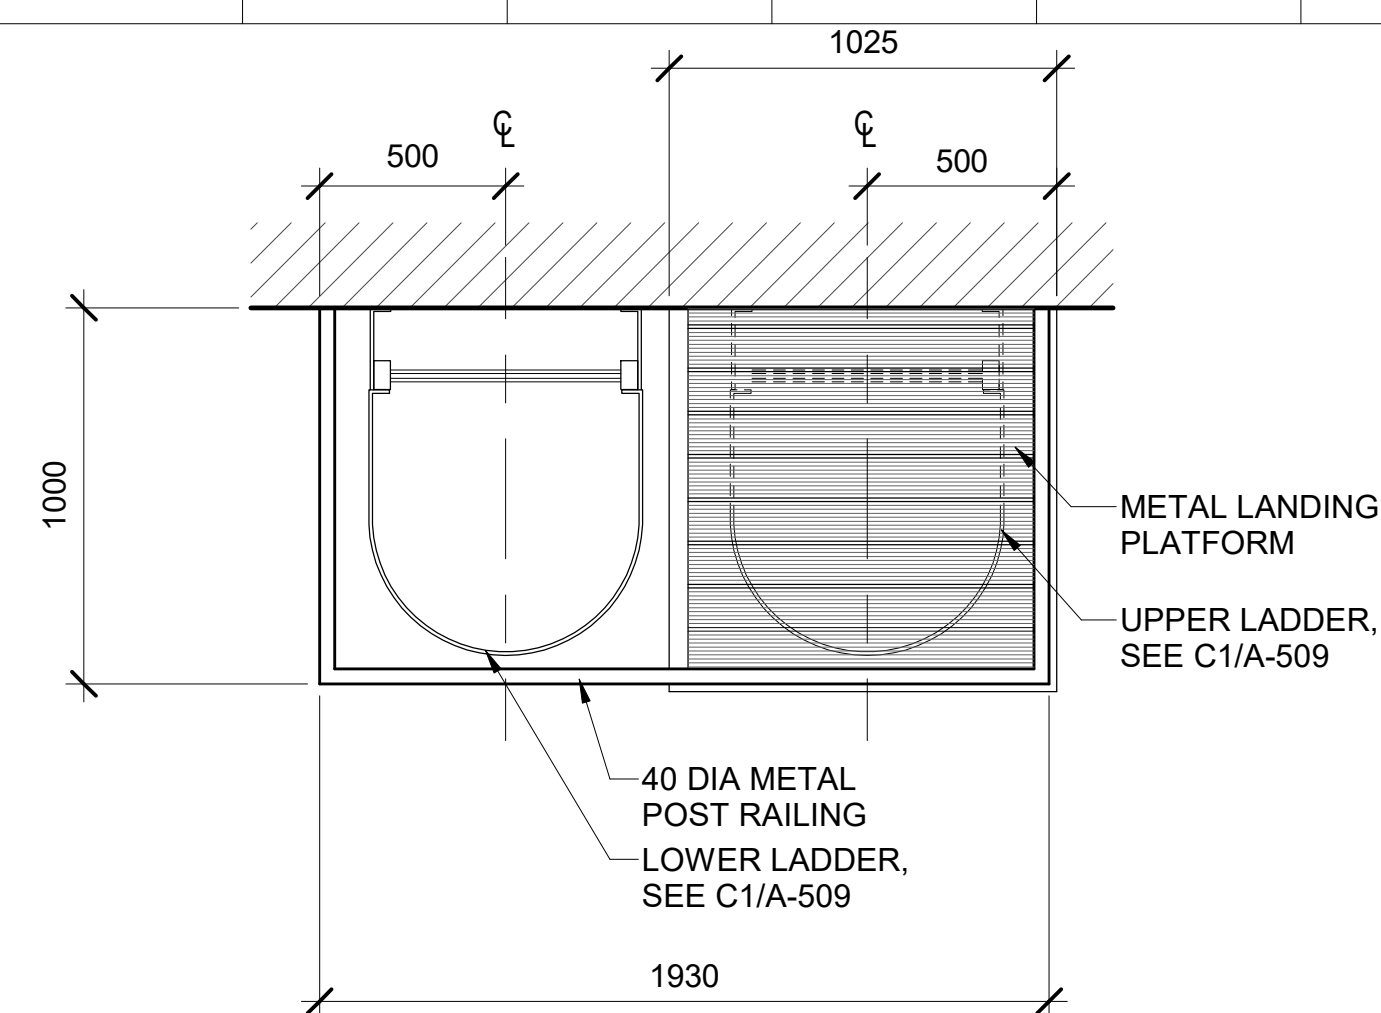


L9 REST PLATFORM PLAN 1 : 20

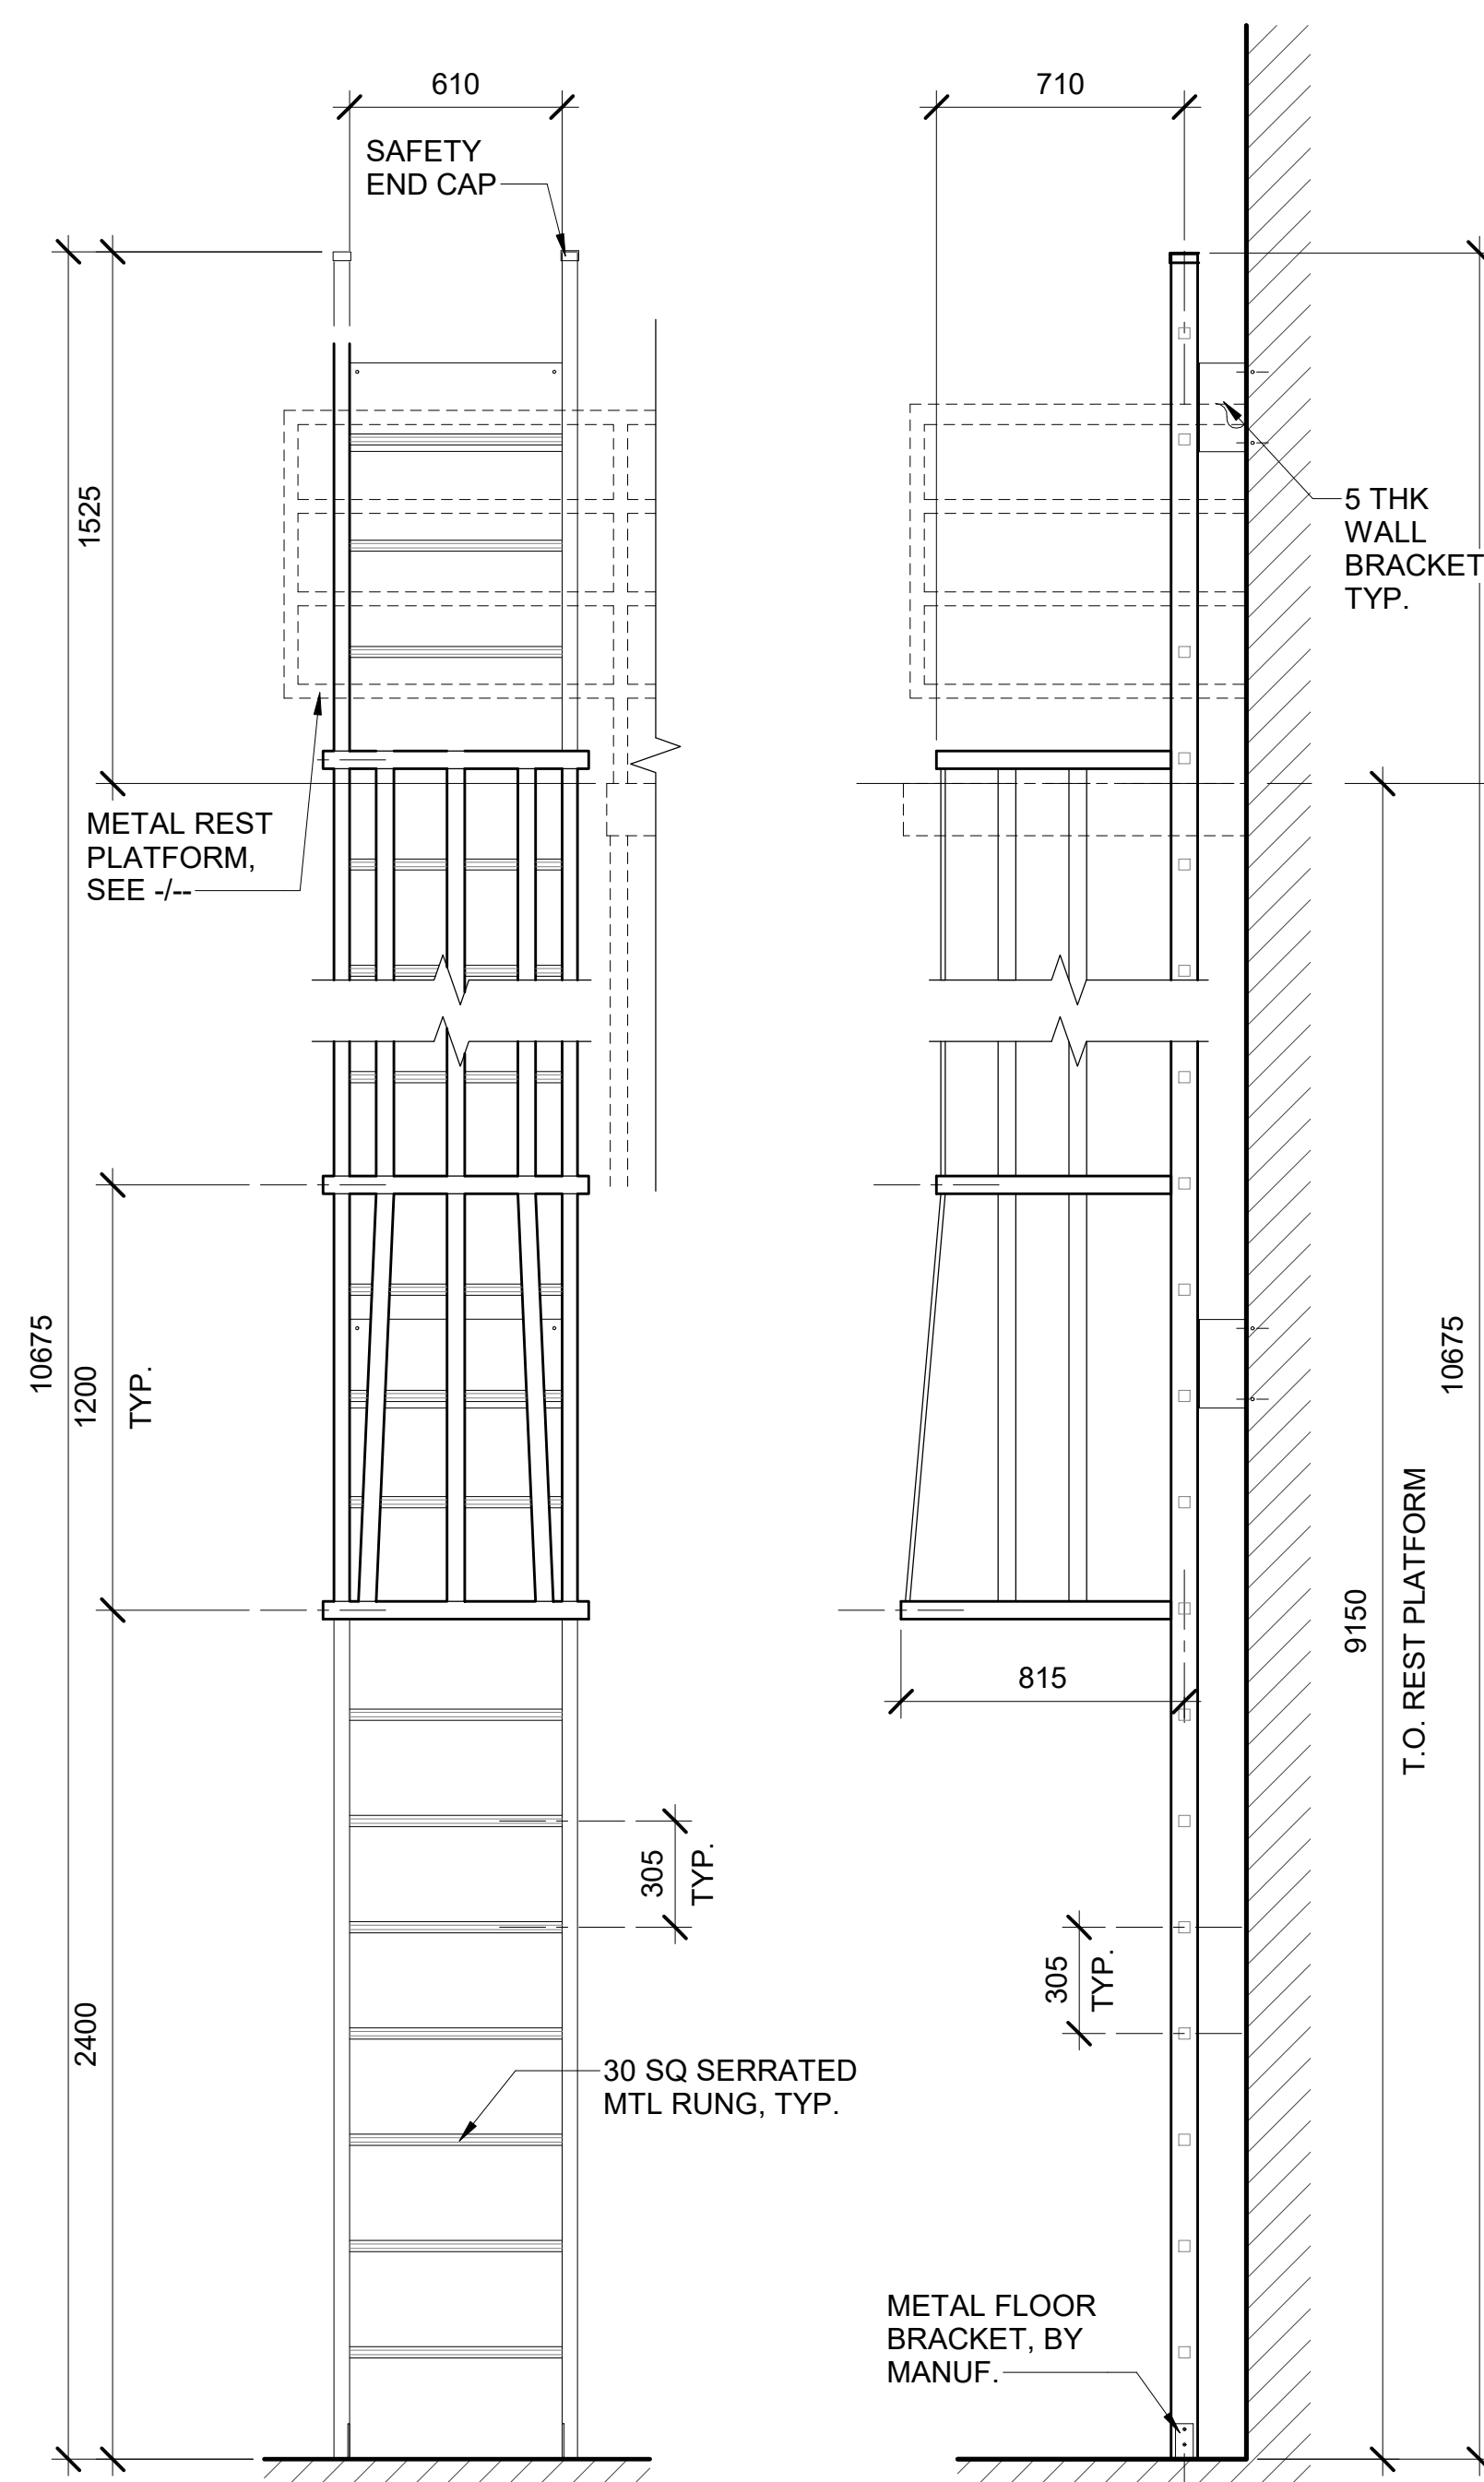

A1 CAGE LADDER

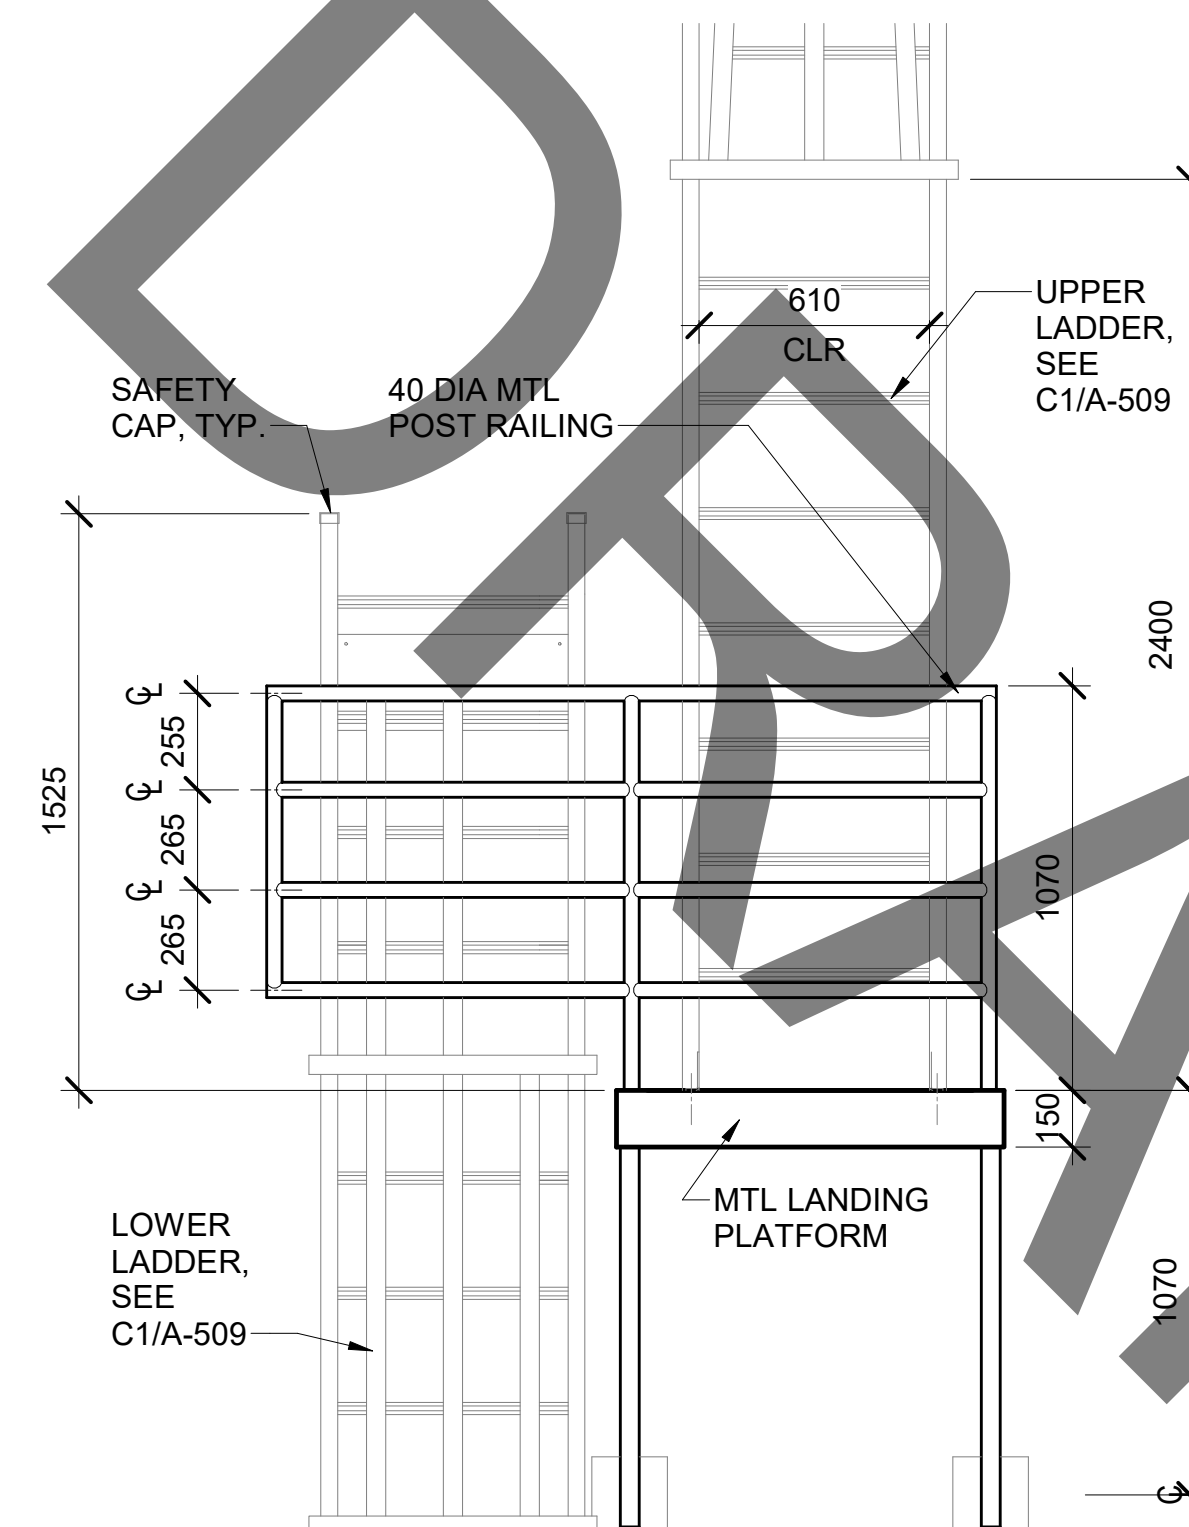

F8 REST PLATFORM ELEVATION

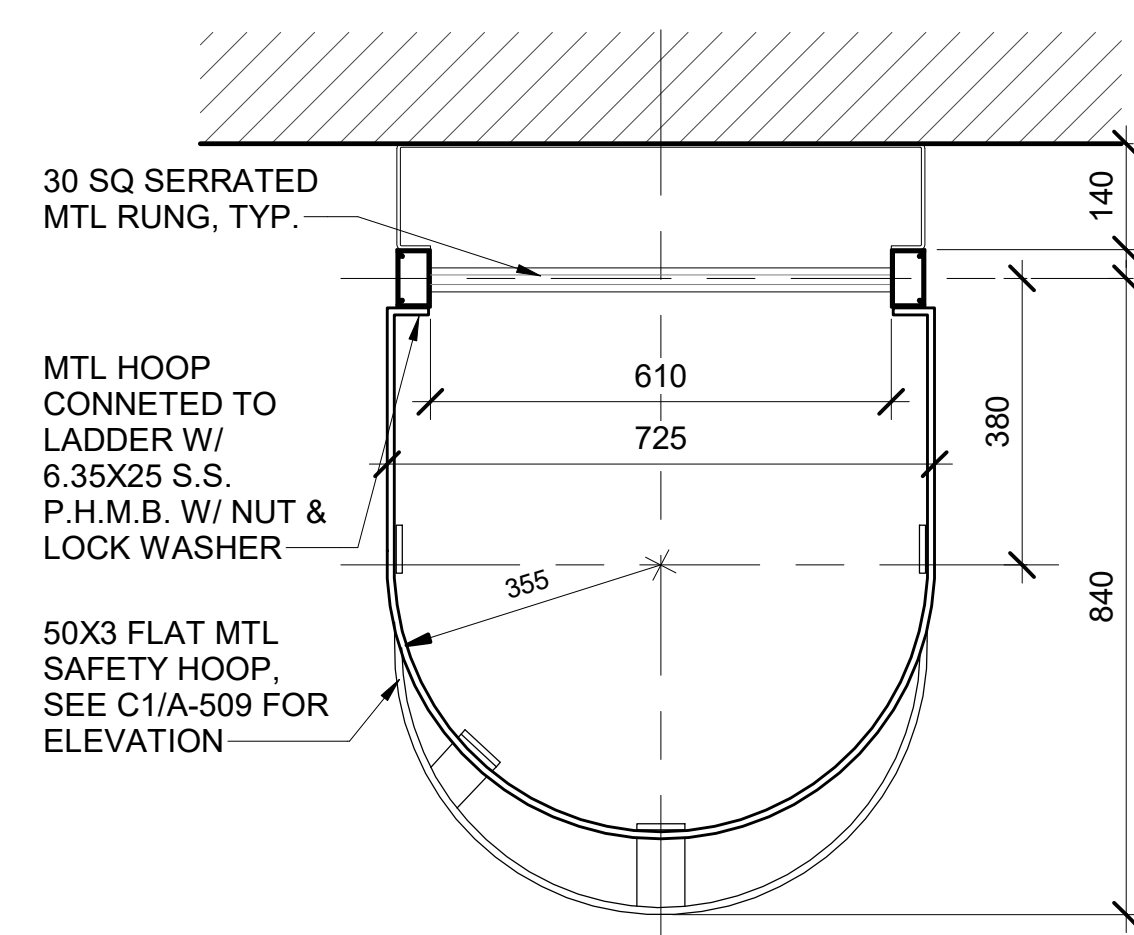


A8 **CAGE PLAN**
1 : 10

US ARMY CORPS OF ENGINEERS JAPAN ENGINEER DISTRICT OKINAWA AREA OFFICE APO AP 96376-5132	DESIGNED BY: K. ELLINGWOOD	ISSUE DATE:
DESIGN PARTNER'S INCORPORATED 1580 MAKALOA STREET, SUITE 1100 HONOLULU HAWAII 96814	DRAWN BY: IROLLO J. MANUJA CHECKED BY: DMONAT'S	SOLICITATION NO.:
	SUBMITTED BY:	CONTRACT NO.:
	SIZE: A/N/A	W912N-17-D-0003


APD AP 96343-5010
FY20 MCA PN17833 VEHICLE MAINTENANCE SHOP

SHEET ID

A-753

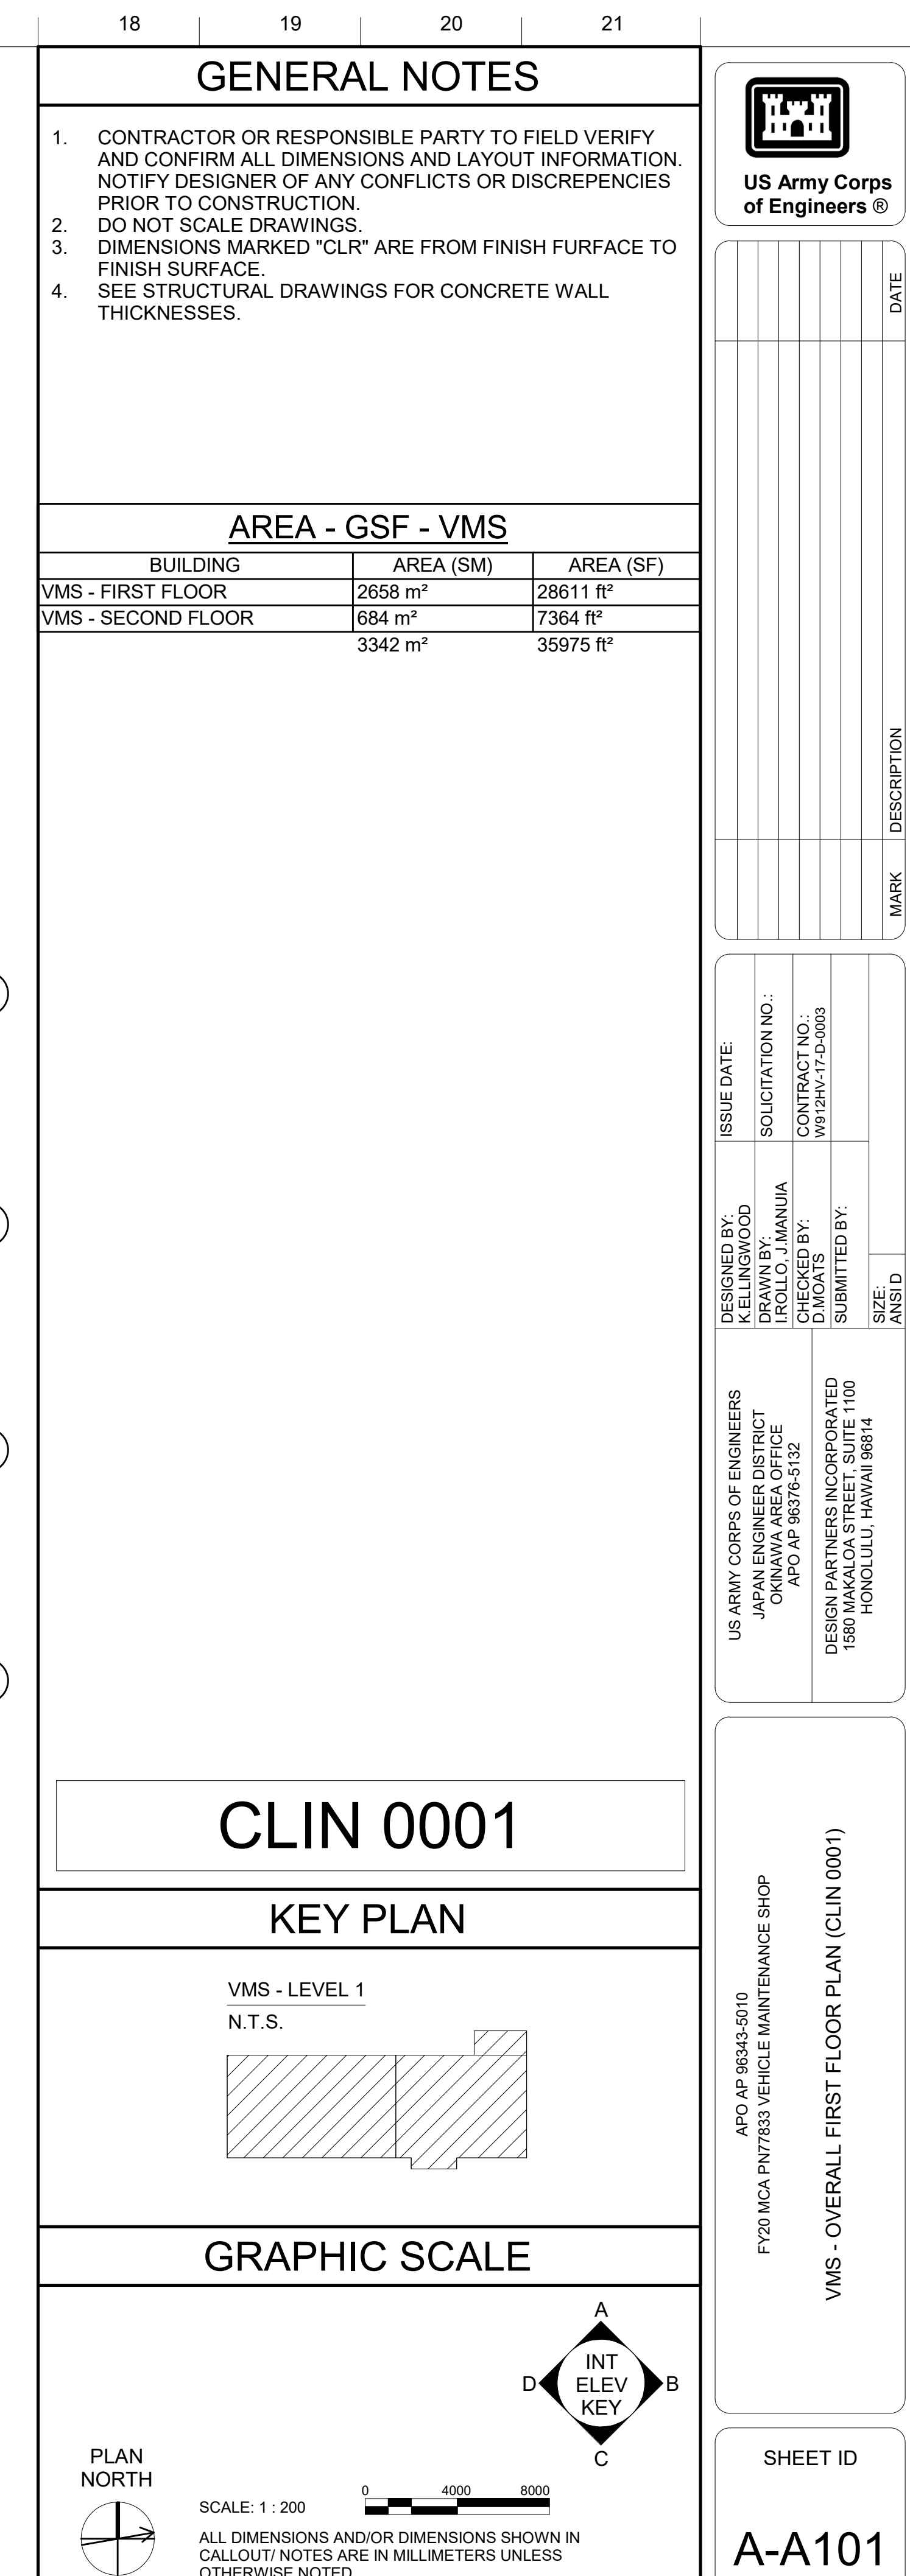



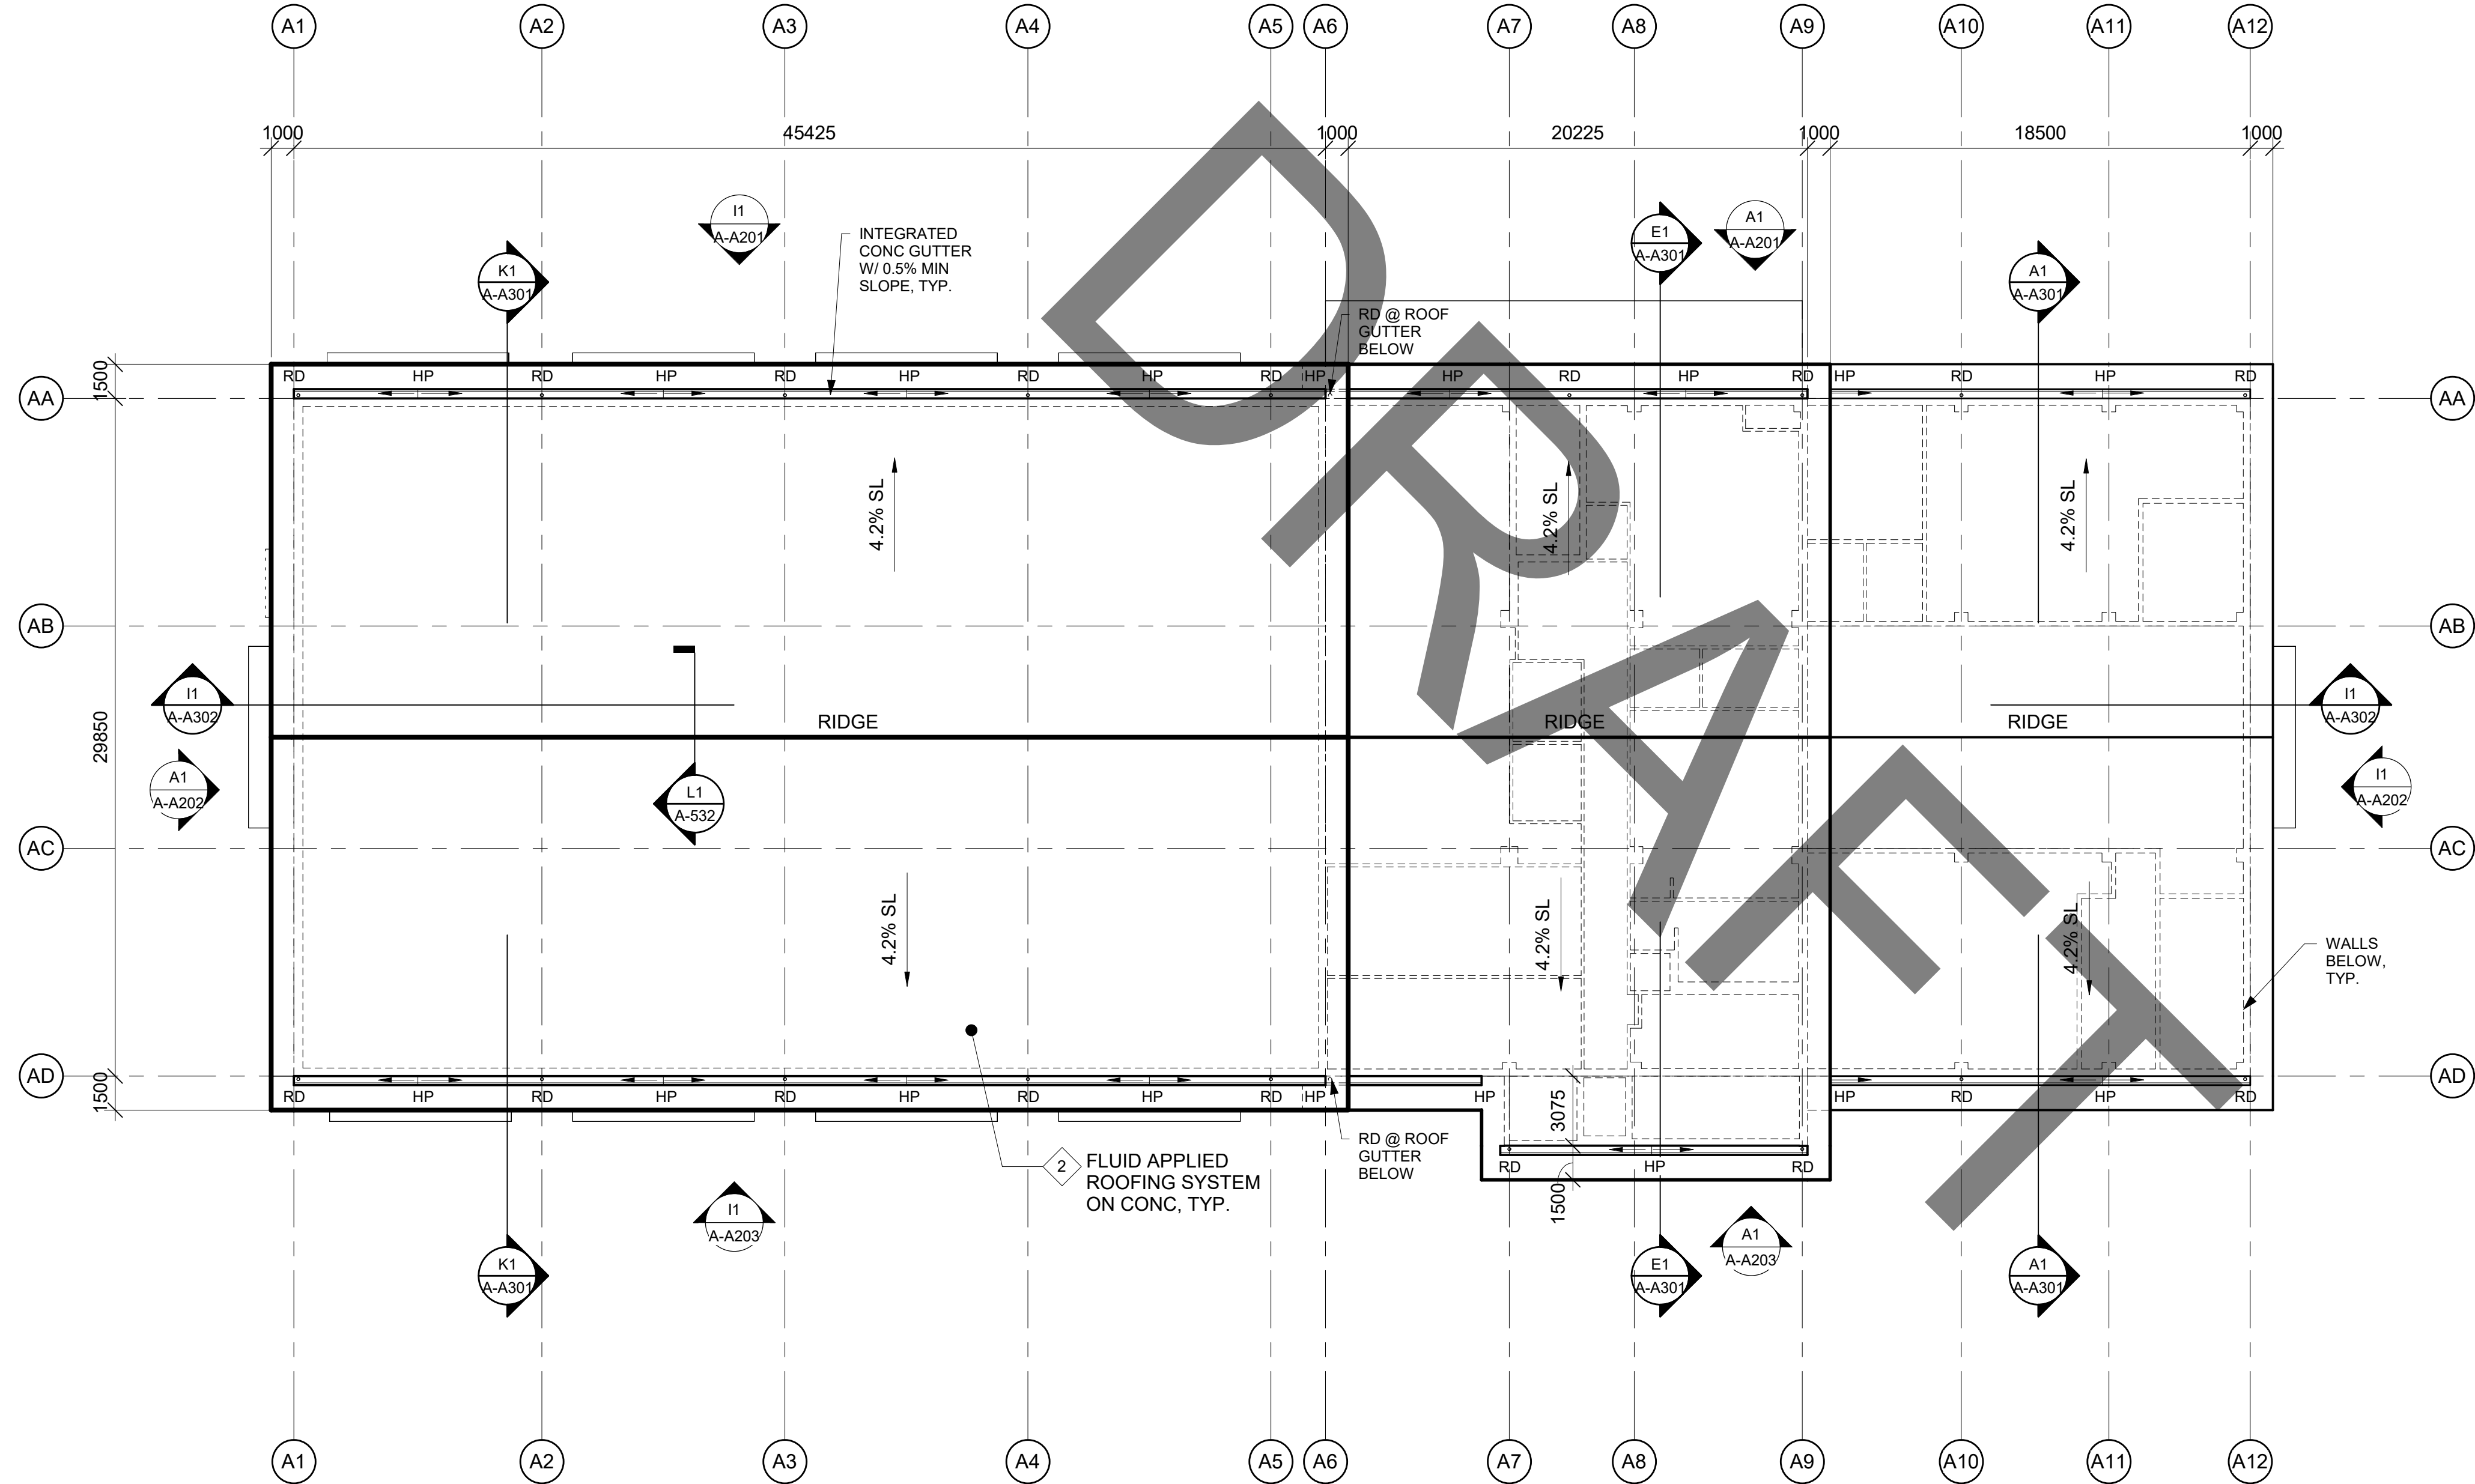

1. PRIMARY ROOFING TO BE FLUID APPLIED ELASTOMERIC ROOFING.
2. ROOFING SUBCONTRACTOR TO VERIFY ALL DIMENSIONS AND CONDITIONS ON SITE.
3. ROOF SLOPE SHALL MAINTAIN SLOPE AS NOTED OVER THE ENTIRE ROOF AREA.
4. ROOF GUTTERS SHALL MAINTAIN A MINIMUM 0.5:10 SLOPE TO ROOF DRAINS.
5. PAINT ALL ROOF TOP EQUIPMENT, ACCESSORIES AND PENETRATIONS TO MATCH ROOF.
6. REFER TO ELECTRICAL FOR LIGHTING PROTECTION LAYOUT.
7. REFER TO REFLECTED CEILING PLANS FOR CONCRETE EYEBROW DIMENSIONS.
8. PROVIDE PERMANENT ROOF ANCHOR FALL ARREST SYSTEM AS REQUIRED PER OSHA. CONTRACTOR TO RETAIN A COMPANY SPECIALIZING IN FALL PROTECTION SYSTEMS TO DESIGN, SUPPLY, INSTALL, AND CERTIFY THE ROOF ANCHOR FALL ARREST SYSTEM.

[illegible]

DESIGNED BY: KELLINGWOOD 1000 W. 5TH AVE TOLLO, ID 83450 PHONE 208-325-1100	ISSUE DATE: 12/1/83
US ARMY CORPS OF ENGINEERS JAPAN ENGINEER DISTRICT OKINAWA AREA OFFICE APO AF 96376-0132	SOLICITATION NO.: W912HW-77-D-0003
DESIGN PARTNERS INCORPORATED 1580 MAKALOA STREET, SUITE 1100 HONOLULU, HAWAII 96814	CHECKED BY: D.MOATS
SIZE: ANSI D	CONTRACT NO.: W912HW-77-D-0003

Autodesk Docs://SSFM JED IDC VEHICLE MAINTENANCE SHOP/511758_TEMF_ARCH_v2022.rvt

File Path:

Plot Date: 12/17/2025 5:18:49 AM

INTERMEDIATE DESIGN

KEY PLAN

N.T.S.



A diamond-shaped diagram with a black border. Inside the diamond is a white circle containing the text "INT ELEV KEY" in black, stacked vertically. The four vertices of the diamond are labeled with black capital letters: "A" at the top, "B" at the right, "C" at the bottom, and "D" at the left.


ALL DIMENSIONS AND/OR DIMENSIONS SHOWN IN
CALLOUT/ NOTES ARE IN MILLIMETERS UNLESS
OTHERWISE NOTED.

FY20 MCA PN77833 VEHICLE MAINTENANCE SHOP


VMS - OVERALL ROOF PLAN (CLIN 0001)

SHEET ID


A-A103

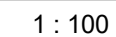


INTERMEDIATE DESIGN

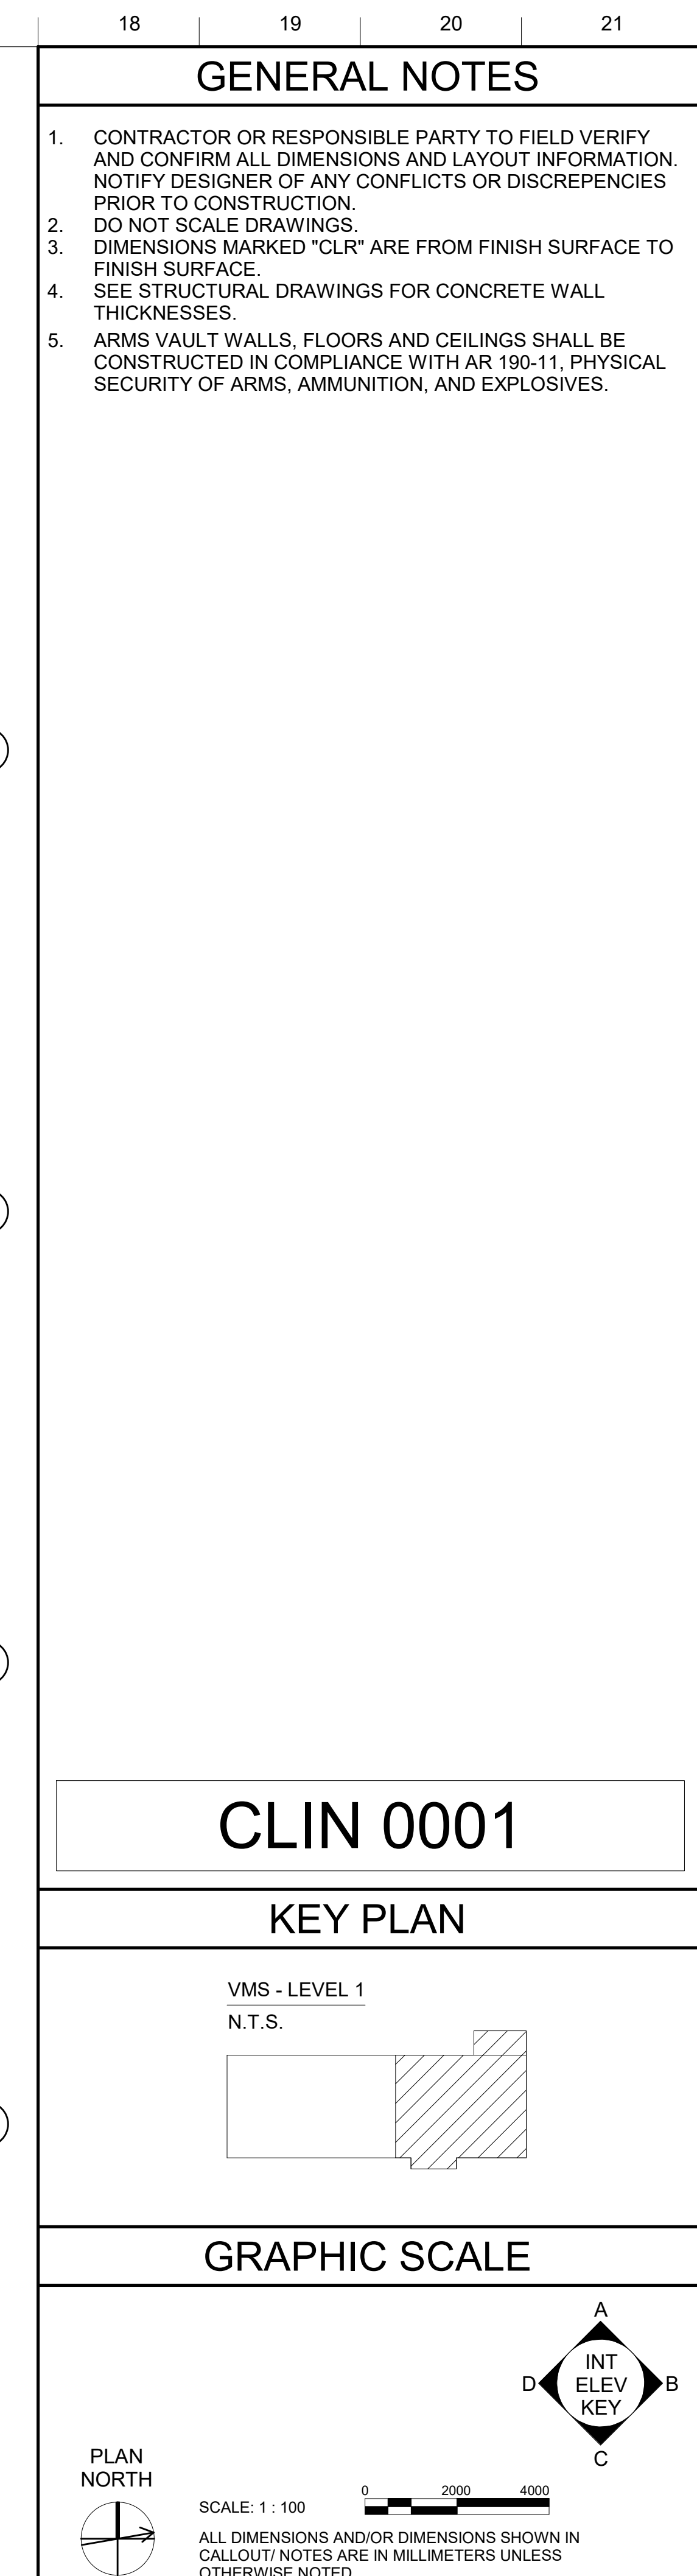


APO AP 96345-5010 FY20 MCA PN77833 VEHICLE MAINTENANCE SHOP VMS - PARTIAL FIRST FLOOR PLAN - ZONE B (CLIN 0001)		SHEET ID A-A112	
US ARMY CORPS OF ENGINEERS JAPAN ENGINEER DISTRICT OKINAWA AREA OFFICE APO AP 96376-5132		DESIGNED BY: KELLINGWOOD DRAWN BY: MANUJA CHECKED BY: D.MCATS SUBMITTED BY:	
DESIGN PARTNERS INCORPORATED 1580 MAKALOA STREET, SUITE 1100 HONOLULU, HAWAII 96814		ISSUE DATE: SOLICITATION NO.: CONTRACT NO.: WO 12HV-17-D-0003 SIZE: ANSI D	
		MARK DESCRIPTION DATE	

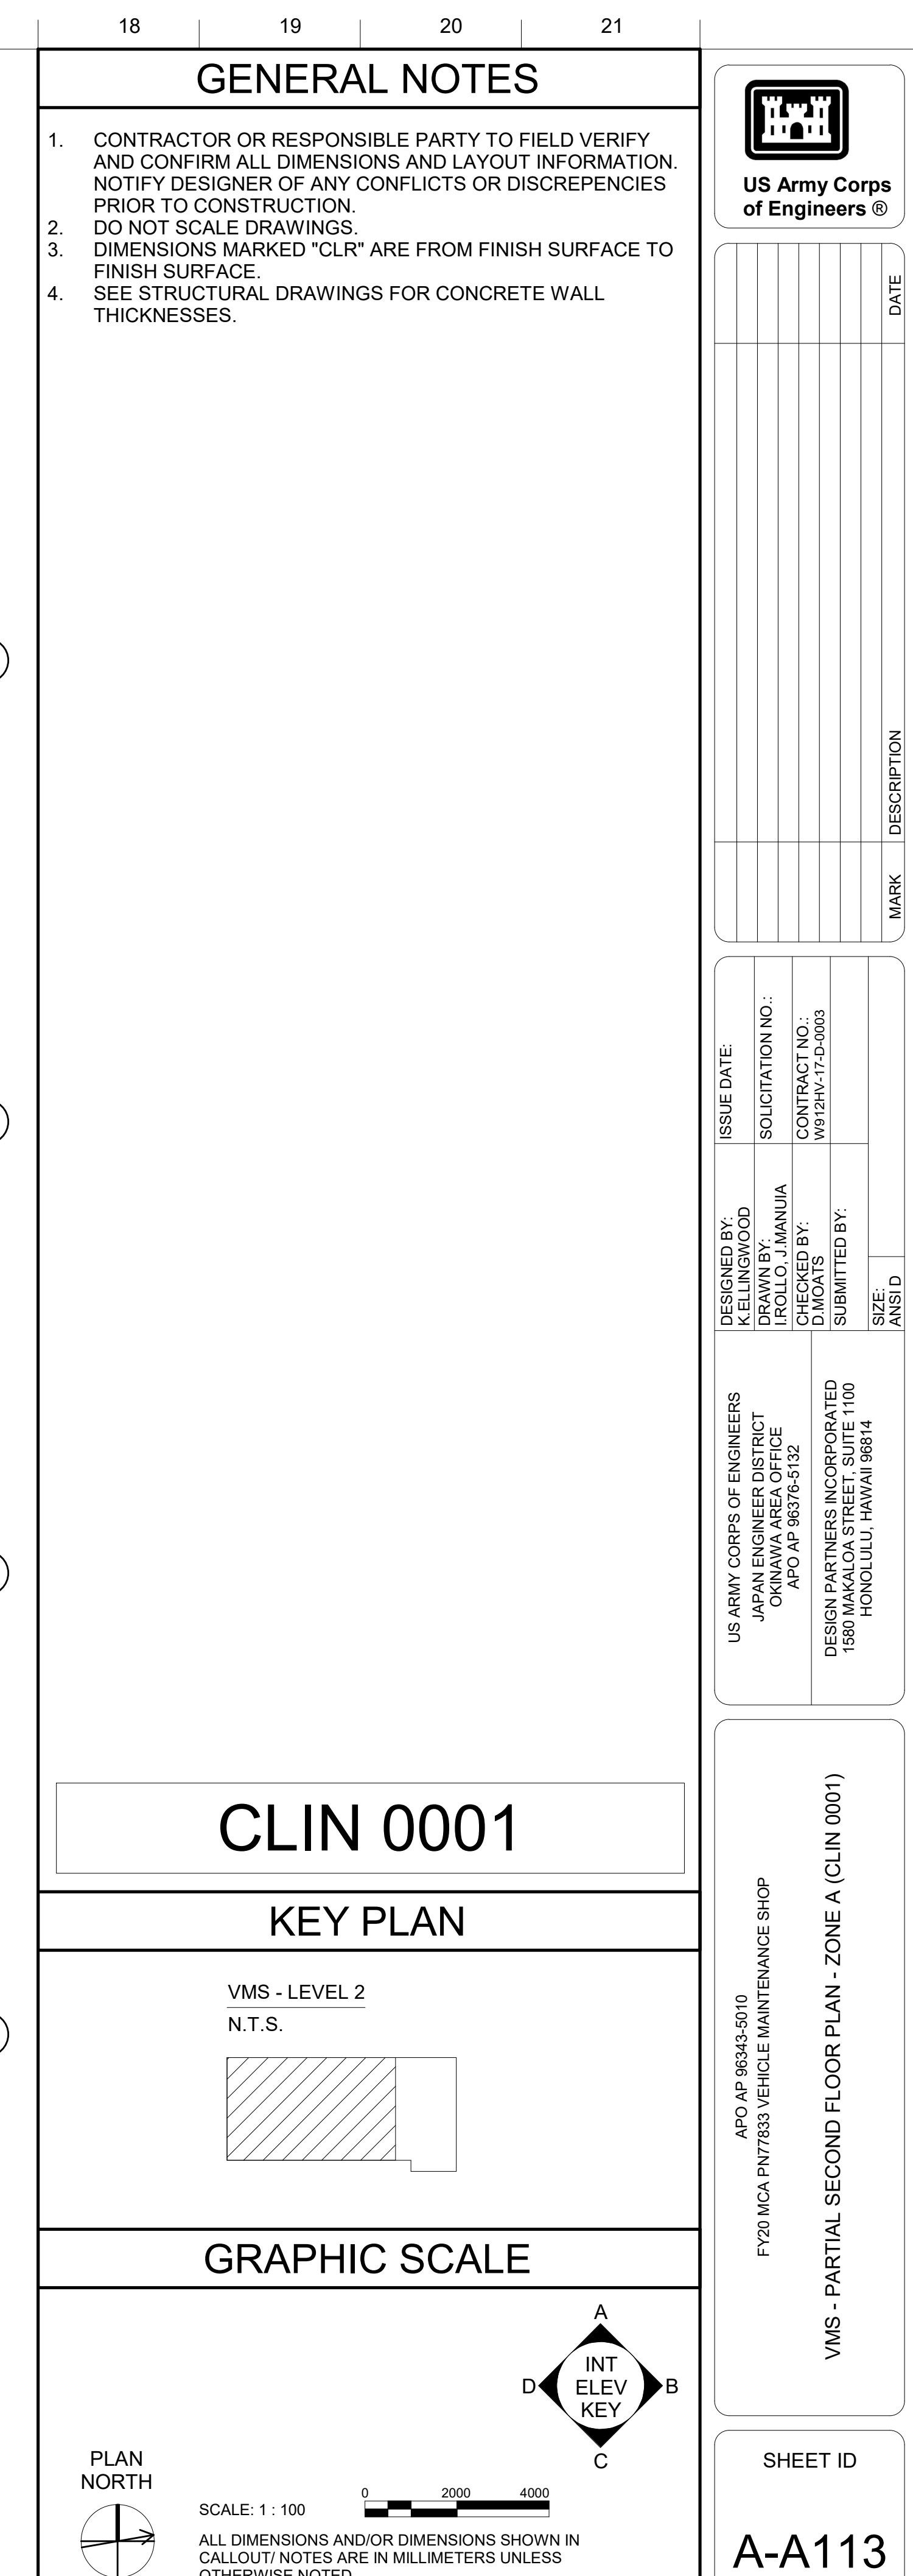

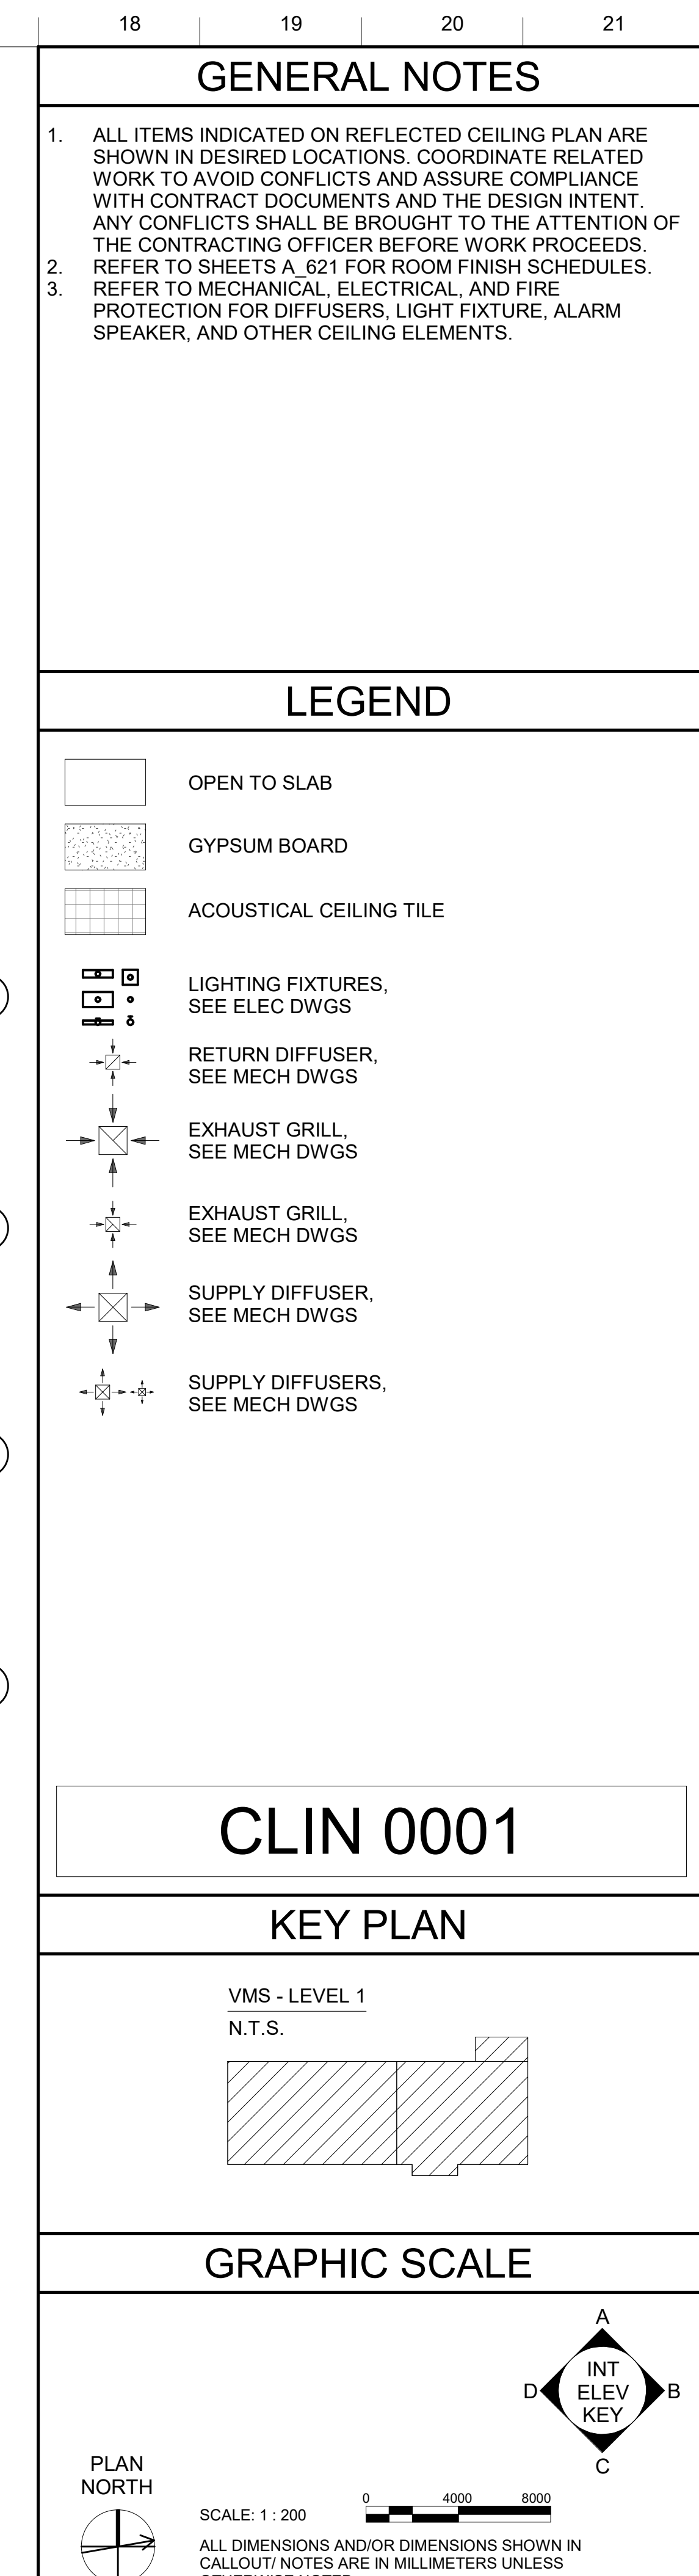

[illegible]

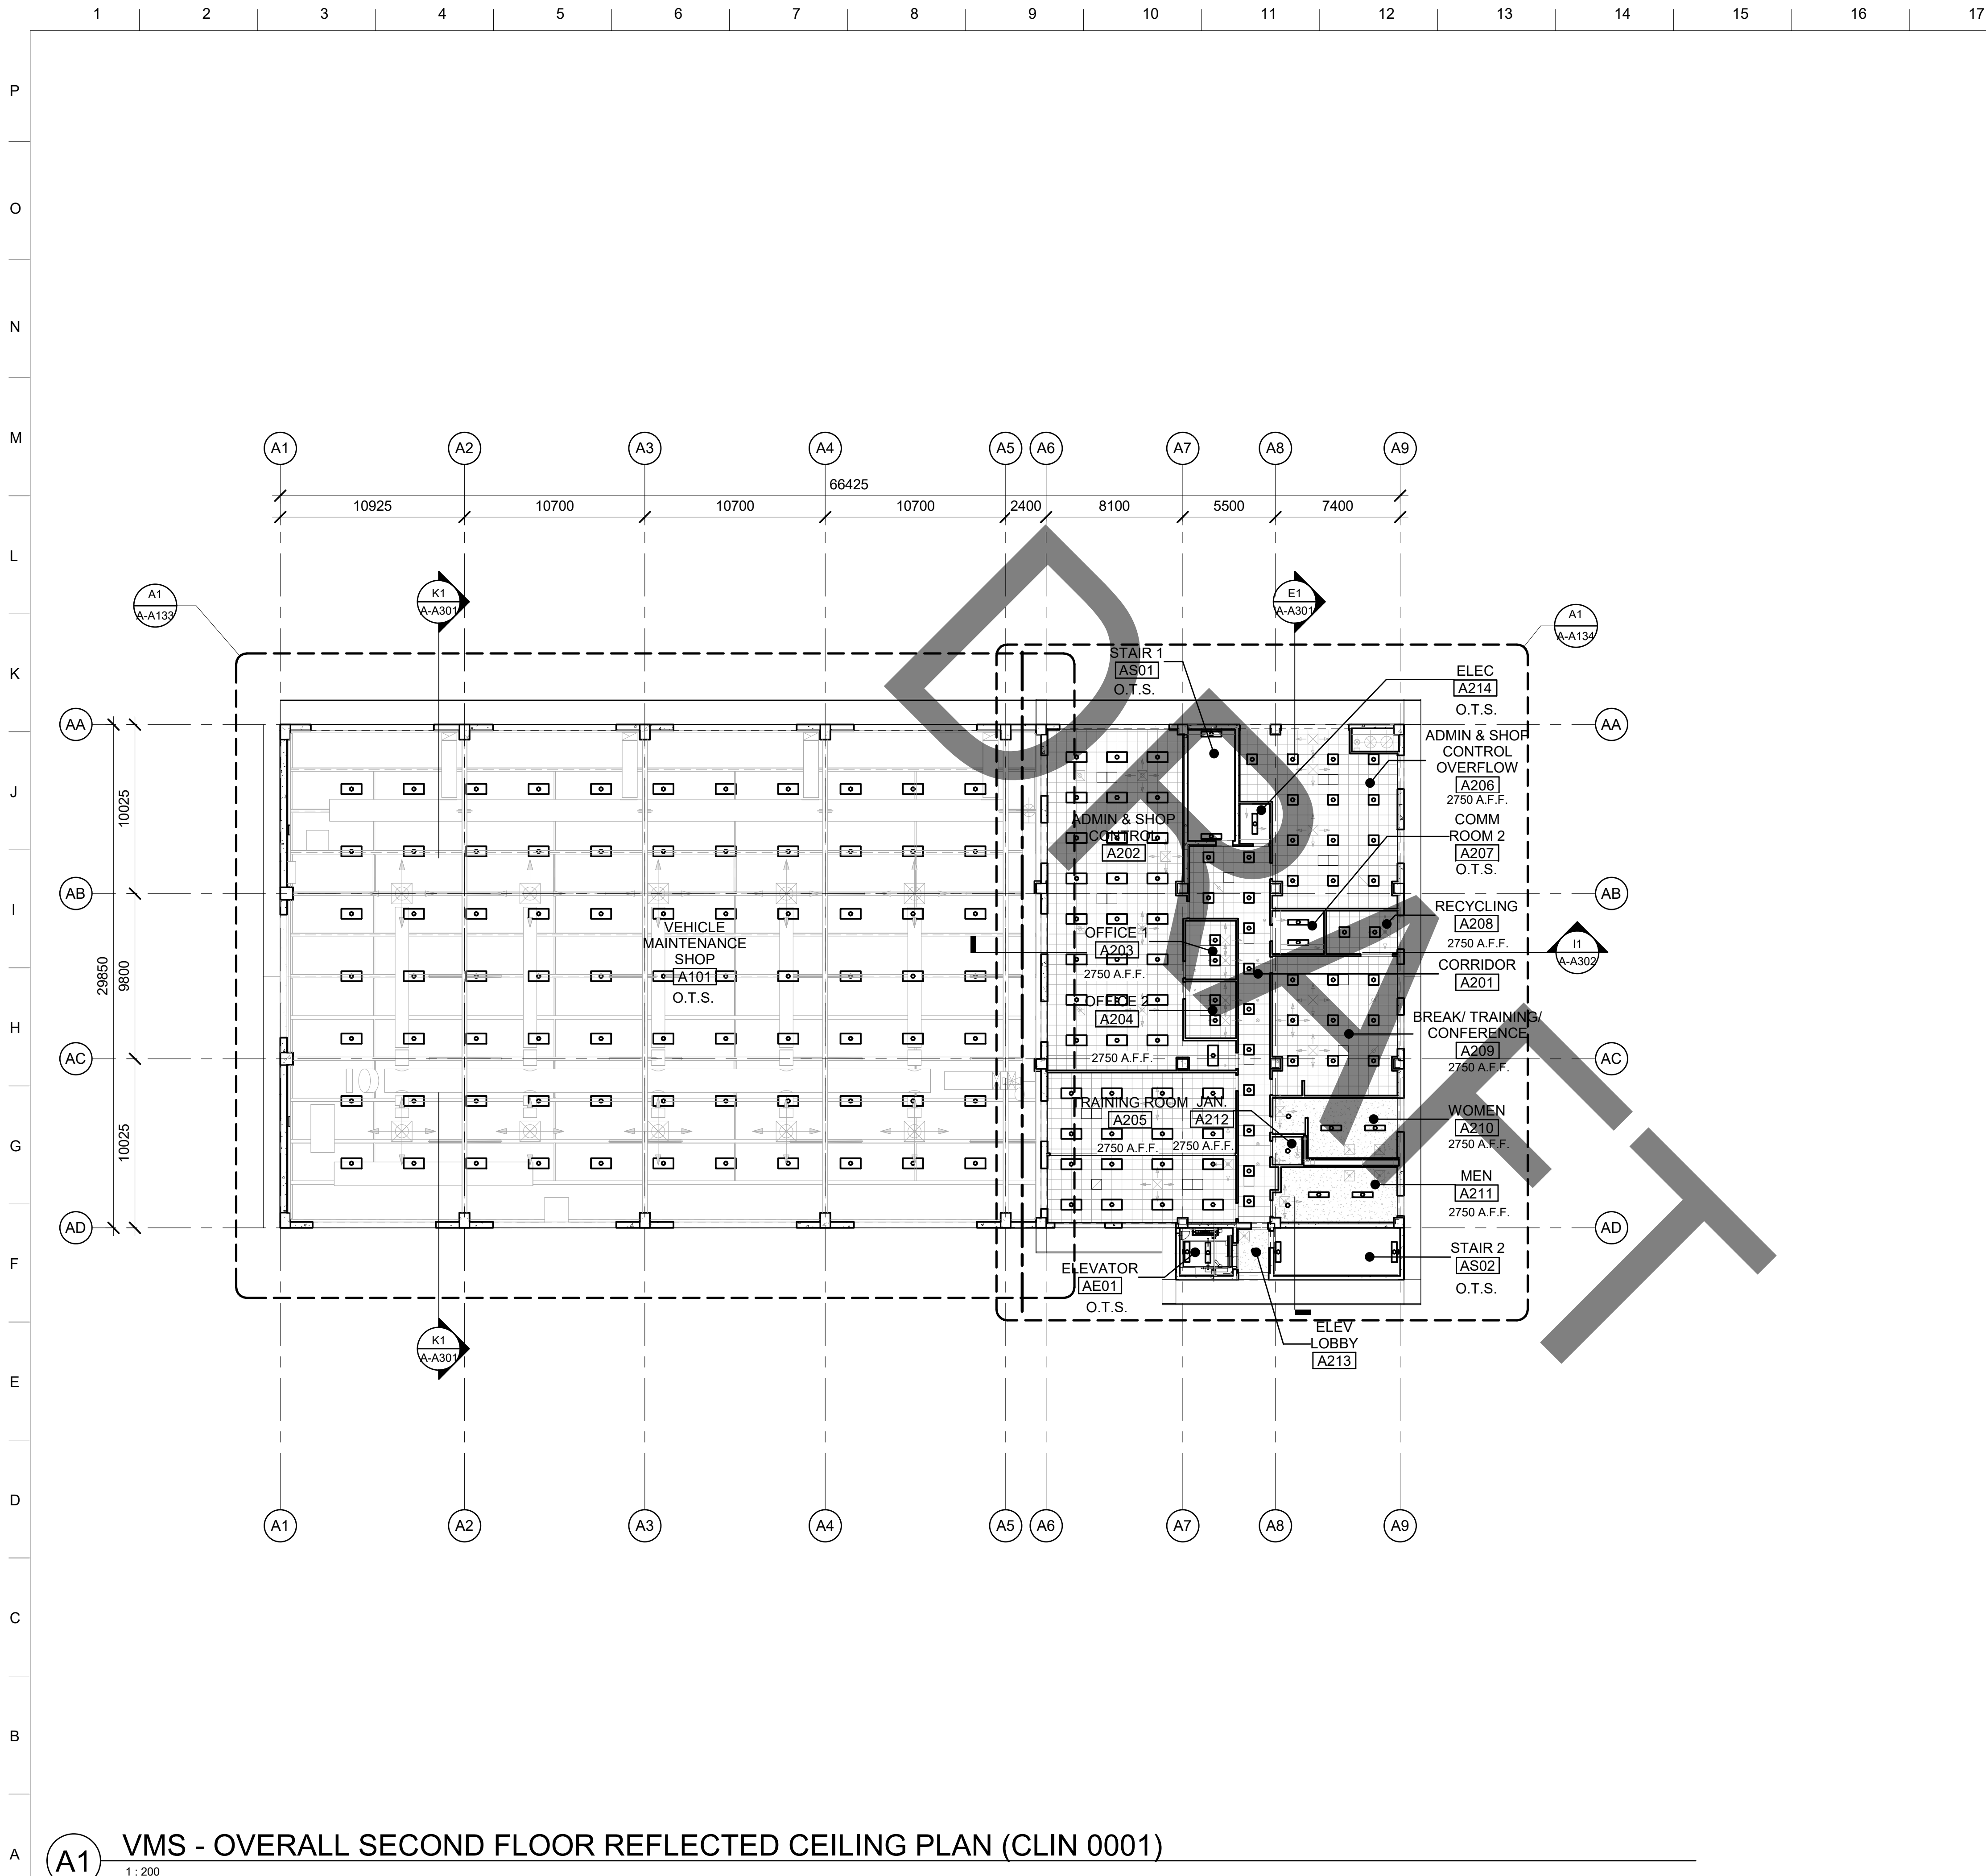

A1 VMS - OVERALL SECOND FLOOR REFLECTED CEILING PLAN (CLIN 0001)

GENERAL NOTES

- ALL ITEMS INDICATED ON REFLECTED CEILING PLAN ARE SHOWN IN DESIRED LOCATIONS. COORDINATE RELATED WORK TO AVOID CONFLICTS AND ASSURE COMPLIANCE WITH CONTRACT DOCUMENTS AND THE DESIGN INTENT. ANY CONFLICTS SHALL BE BROUGHT TO THE ATTENTION OF THE CONTRACTING OFFICER BEFORE WORK PROCEEDS.
- REFER TO SHEETS A. 621 FOR ROOM FINISH SCHEDULES.
- REFER TO MECHANICAL, ELECTRICAL, AND FIRE PROTECTION FOR DIFFUSERS, LIGHT FIXTURE, ALARM SPEAKER, AND OTHER CEILING ELEMENTS.



US Army Corps
of Engineers ®


LEGEND

- OPEN TO SLAB
- GYPSUM BOARD
- ACOUSTICAL CEILING TILE
- LIGHTING FIXTURES, SEE ELEC DWGS
- RETURN DIFFUSER, SEE MECH DWGS
- EXHAUST GRILL, SEE MECH DWGS
- EXHAUST GRILL, SEE MECH DWGS
- SUPPLY DIFFUSER, SEE MECH DWGS
- SUPPLY DIFFUSERS, SEE MECH DWGS

CLIN 0001

KEY PLAN

VMS - LEVEL 2
N.T.S.

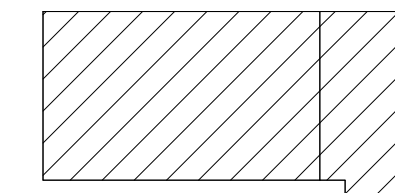

GRAPHIC SCALE


PLAN
NORTH



SCALE: 1 : 200

0 4000 8000

ALL DIMENSIONS AND/OR DIMENSIONS SHOWN IN
CALLOUT/ NOTES ARE IN MILLIMETERS UNLESS
OTHERWISE NOTED.

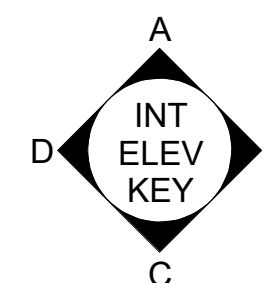

APO AP 96343-5010
FY20 MCA PN77833 VEHICLE MAINTENANCE SHOP

VMS - OVERALL SECOND FLOOR REFLECTED CEILING PLAN (CLIN 0001)

SHEET ID

A-A122

INTERMEDIATE DESIGN

Plot Date: 12/17/2025 5:19:02 AM


File Path:

Autodesk Docs/USPM/EDDC/VEHICLE MAINTENANCE SHOP/17783_TEMPL/ARCH/0001.dwg









GENERAL NOTES

1. ALL ITEMS INDICATED ON REFLECTED CEILING PLAN ARE SHOWN IN DESIRED LOCATIONS. COORDINATE RELATED WORK TO AVOID CONFLICTS AND ASSURE COMPLIANCE WITH CONTRACT DOCUMENTS AND THE DESIGN INTENT. ANY CONFLICTS SHALL BE BROUGHT TO THE ATTENTION OF THE CONTRACTING OFFICER BEFORE WORK PROCEEDS.
2. REFER TO MECHANICAL, ELECTRICAL, AND FIRE PROTECTION FOR DIFFUSERS, LIGHT FIXTURE, ALARM SPEAKER, AND OTHER CEILING ELEMENTS.

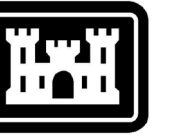[illegible]


LEGEND

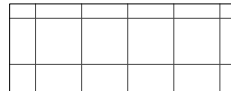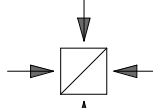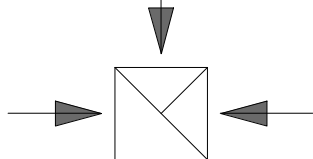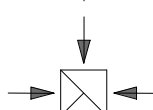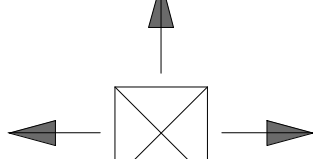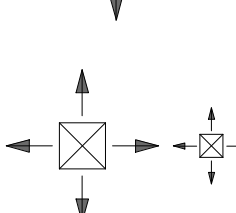- | | |
|---|-------------------------------------|
|  | OPEN TO SLAB |
|  | GYPSUM BOARD |
|  | ACOUSTICAL CEILING TILE |
|  | LIGHTING FIXTURES,
SEE ELEC DWGS |
|  | |
|  | |
|  | RETURN DIFFUSER,
SEE MECH DWGS |
|  | EXHAUST GRILL,
SEE MECH DWGS |
|  | EXHAUST GRILL,
SEE MECH DWGS |
|  | SUPPLY DIFFUSER,
SEE MECH DWGS |
|  | SUPPLY DIFFUSERS,
SEE MECH DWGS |

CLIN 0001

KEY PLAN

VMS - LEVEL 1
N.T.S.

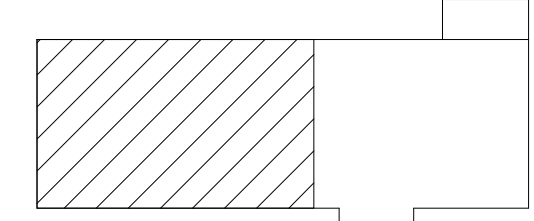


GRAPHIC SCALE



SCALE: 1 : 100



ALL DIMENSIONS AND/OR DIMENSIONS SHOWN IN
CALLOUT/ NOTES ARE IN MILLIMETERS UNLESS
OTHERWISE NOTED.

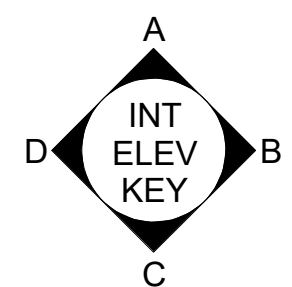

APC AF 36345-5010
FY20 MCA PN7833 VEHICLE MAINTENANCE SHOP

SHEET ID


A-A131

INTERMEDIATE DESIGN

Plot Date: 12/17/2025 5:19:05 AM

File Path:

Autodesk Docs://SSFM JED IDC VEHICLE MAINTENANCE SHOP/511758_TEMF_ARCH_V2022.rvt

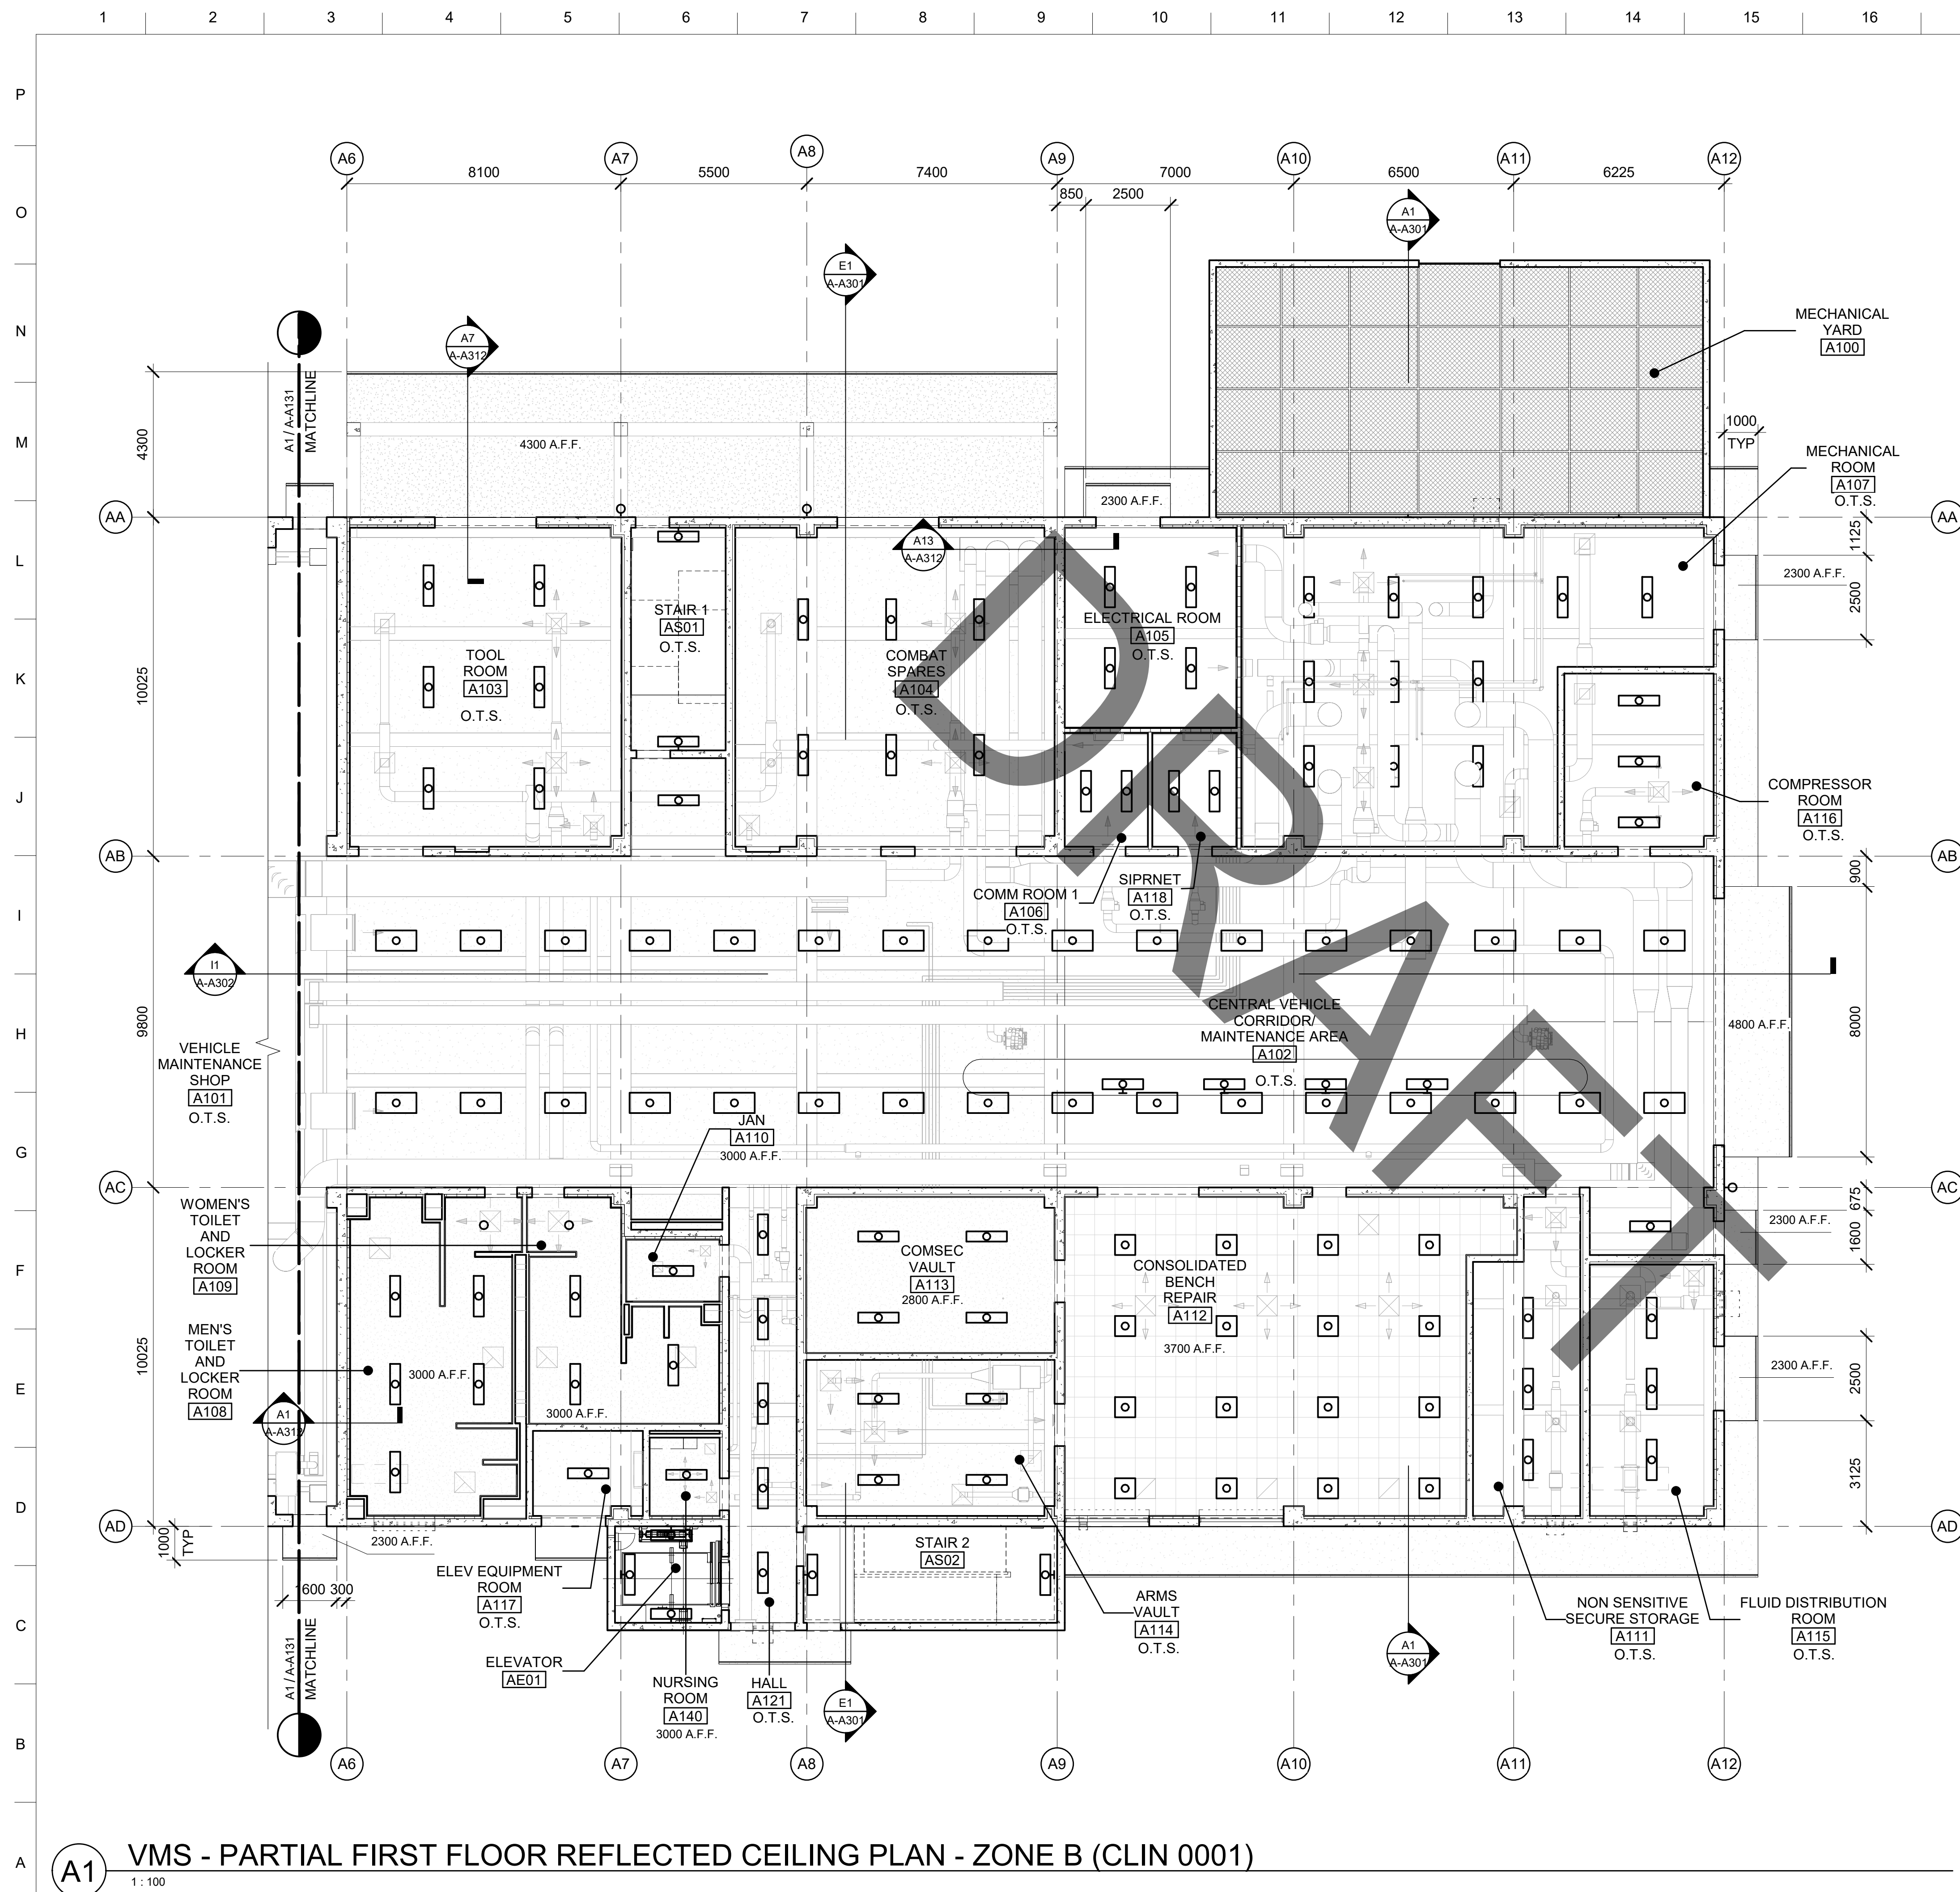


GENERAL NOTES

1. ALL ITEMS INDICATED ON REFLECTED CEILING PLAN ARE SHOWN IN DESIRED LOCATIONS. COORDINATE RELATED WORK TO AVOID CONFLICTS AND ASSURE COMPLIANCE WITH CONTRACT DOCUMENTS AND THE DESIGN INTENT. ANY CONFLICTS SHALL BE BROUGHT TO THE ATTENTION OF THE CONTRACTING OFFICER BEFORE WORK PROCEEDS.
2. REFER TO MECHANICAL, ELECTRICAL, AND FIRE PROTECTION FOR DIFFUSERS, LIGHT FIXTURE, ALARM SPEAKER, AND OTHER CEILING ELEMENTS.



US Army Corps
of Engineers®


LEGEND

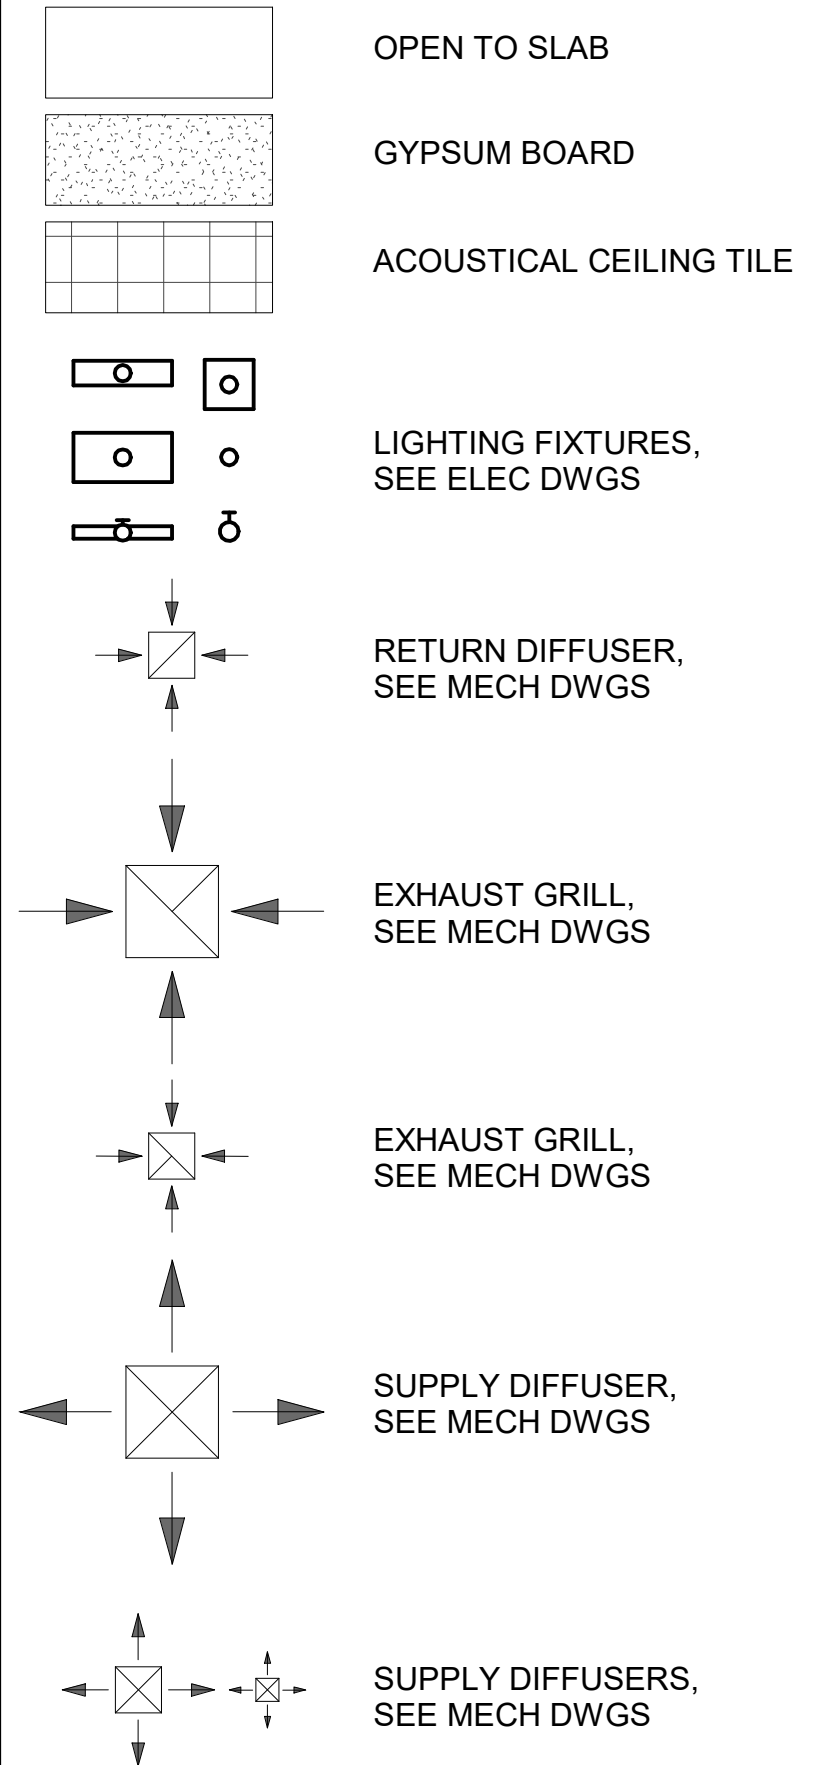

CLIN 0001

KEY PLAN

VMS - LEVEL 1
N.T.S.

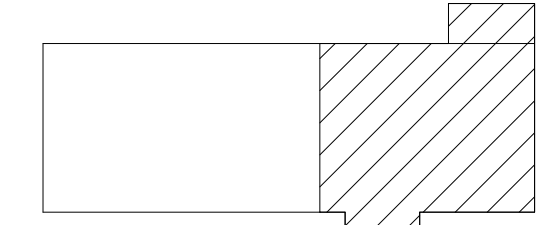


GRAPHIC SCALE



SCALE: 1 : 100

ALL DIMENSIONS AND/OR DIMENSIONS SHOWN IN
CALLOUT/ NOTES ARE IN MILLIMETERS UNLESS
OTHERWISE NOTED.

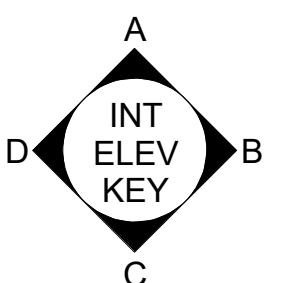

7833 VEHICLE MAINTENANCE SHOP

FY20 MCA PN77833 VEHICLE MAINTENANCE SHOP


SHEET ID

A-A132

INTERMEDIATE DESIGN

Plot Date: 12/17/2025 5:19:08 AM

Autodesk Docs://SSFM JED IDC VEHICLE MAINTENANCE SHOP/511758_TEMF_ARCH_v2022.rvt

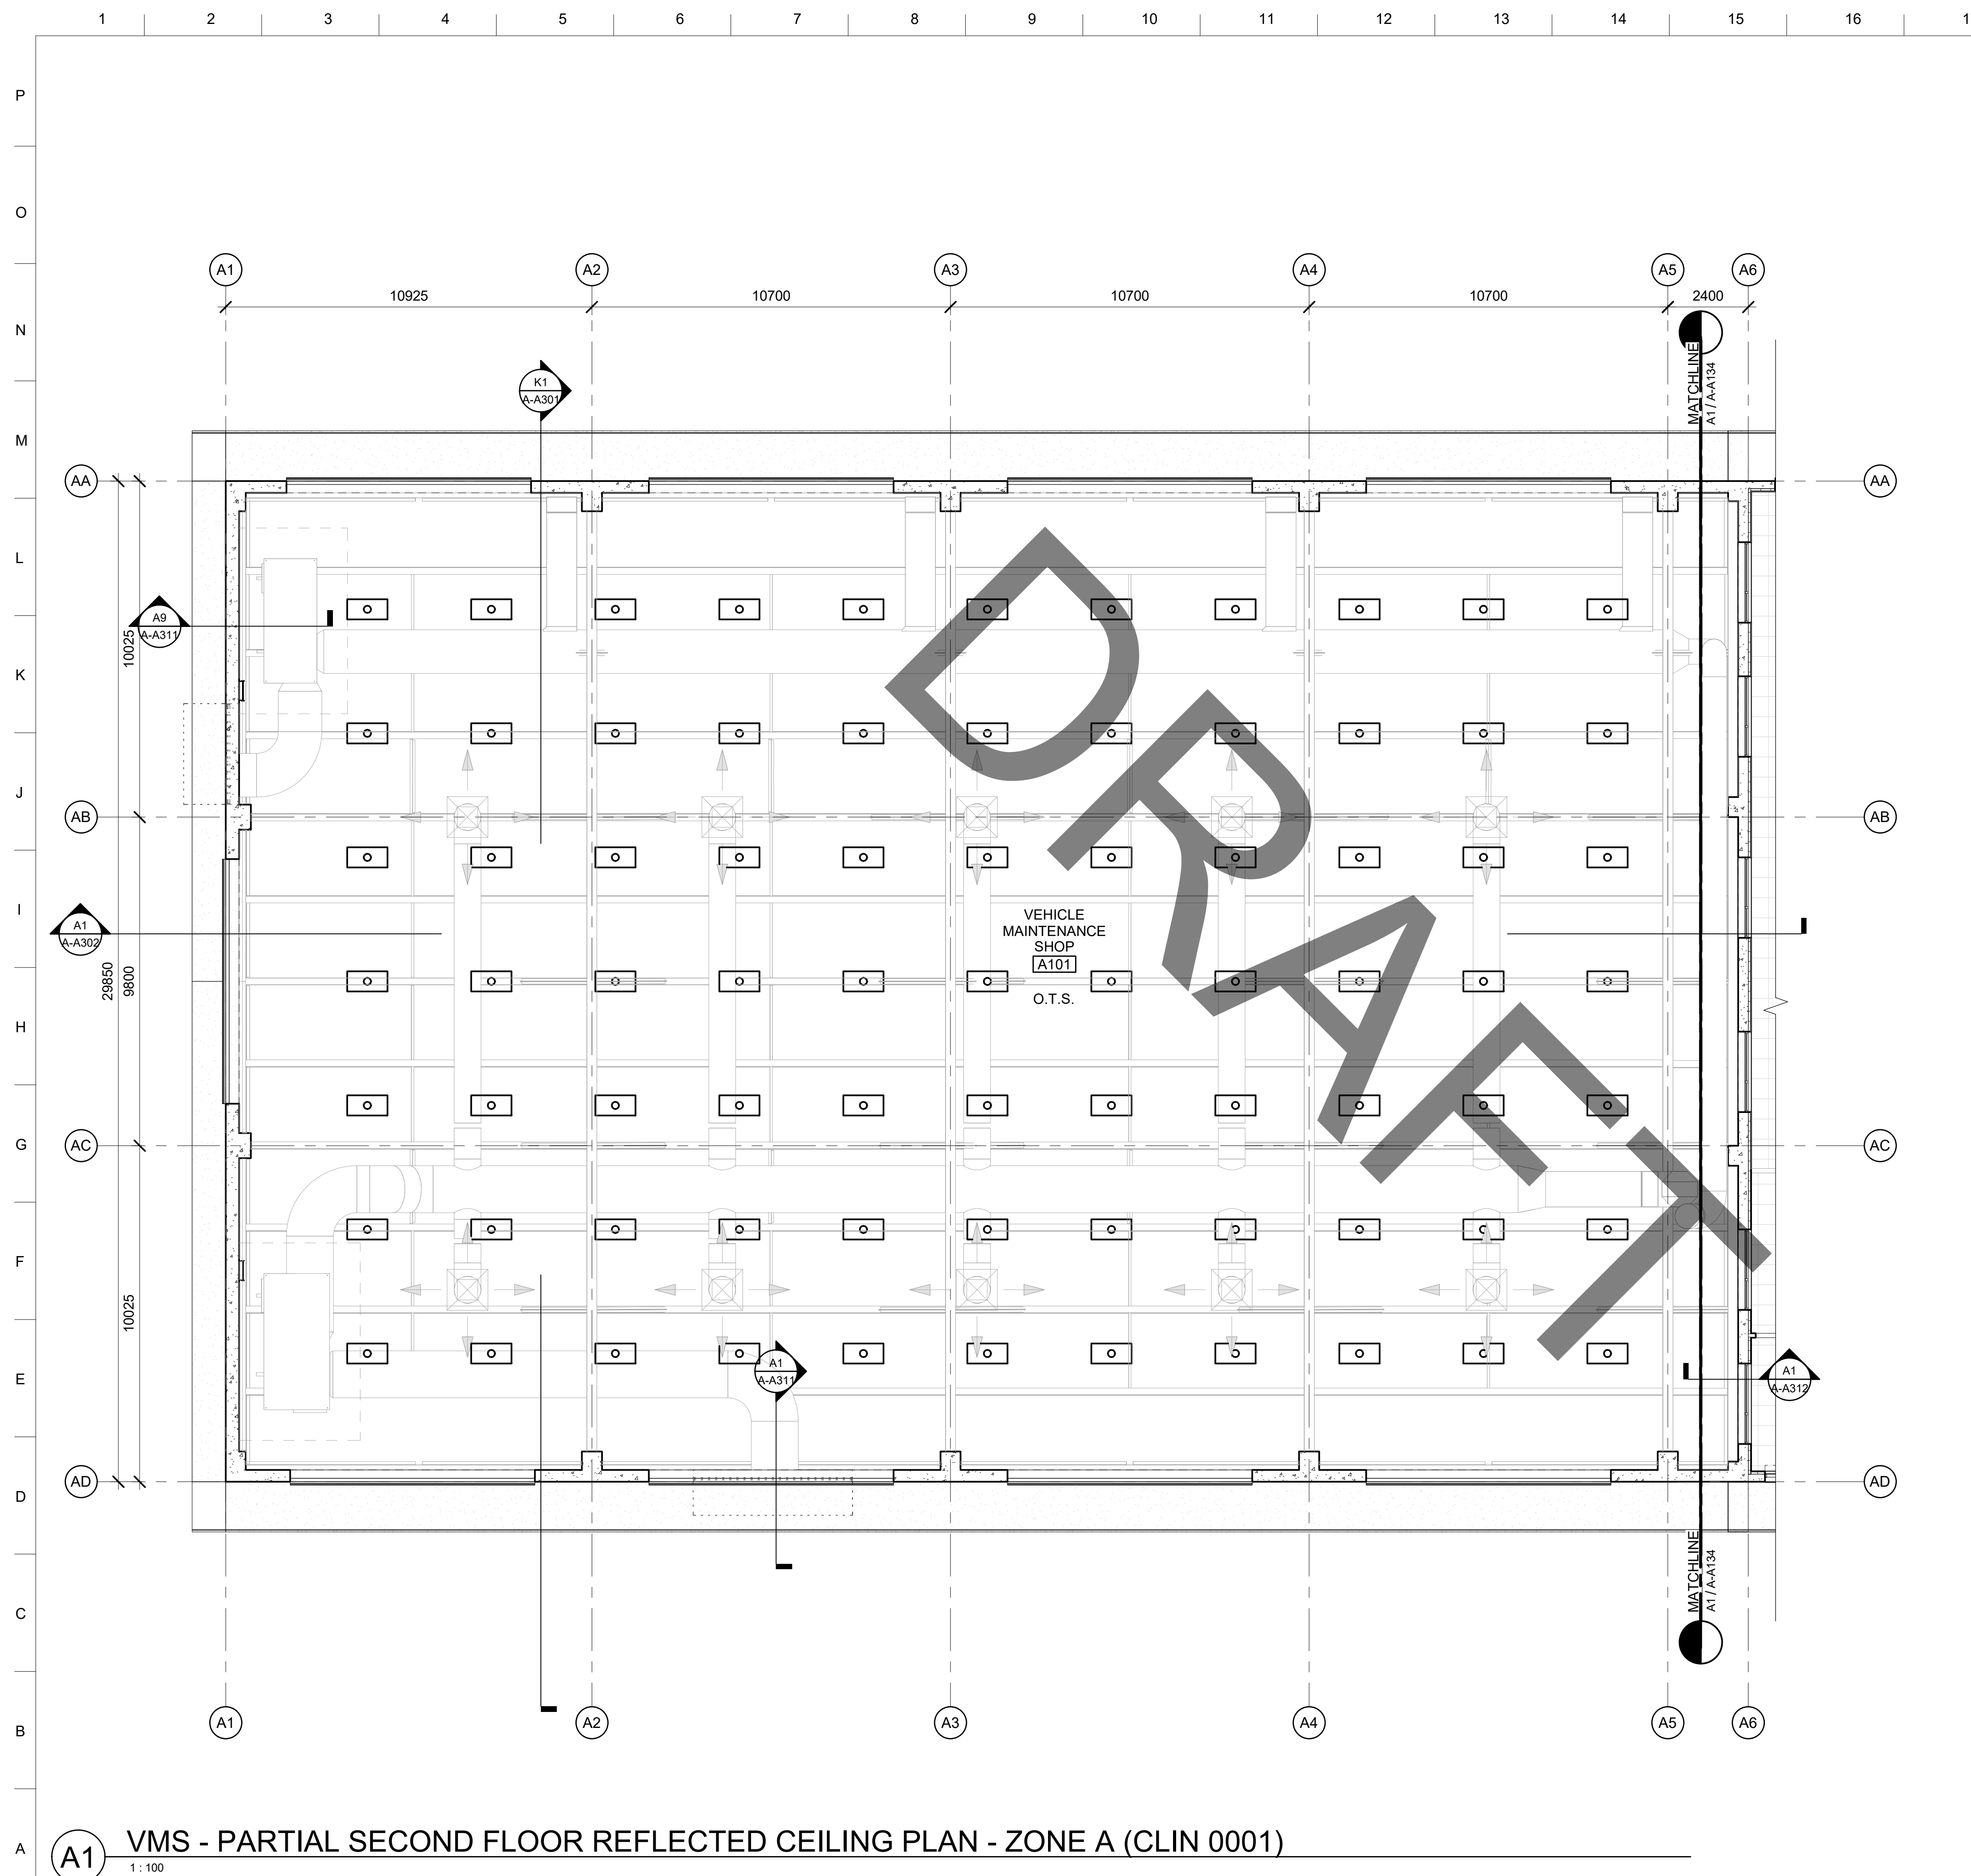


GENERAL NOTES

1. ALL ITEMS INDICATED ON REFLECTED CEILING PLAN ARE SHOWN IN DESIRED LOCATIONS. COORDINATE RELATED WORK TO AVOID CONFLICTS AND ASSURE COMPLIANCE WITH CONTRACT DOCUMENTS AND THE DESIGN INTENT. ANY CONFLICTS SHALL BE BROUGHT TO THE ATTENTION OF THE CONTRACTING OFFICER BEFORE WORK PROCEEDS.
2. REFER TO MECHANICAL, ELECTRICAL, AND FIRE PROTECTION FOR DIFFUSERS, LIGHT FIXTURE, ALARM SPEAKER, AND OTHER CEILING ELEMENTS.



**U.S. Army Corps
Engineers®**


LEGEND

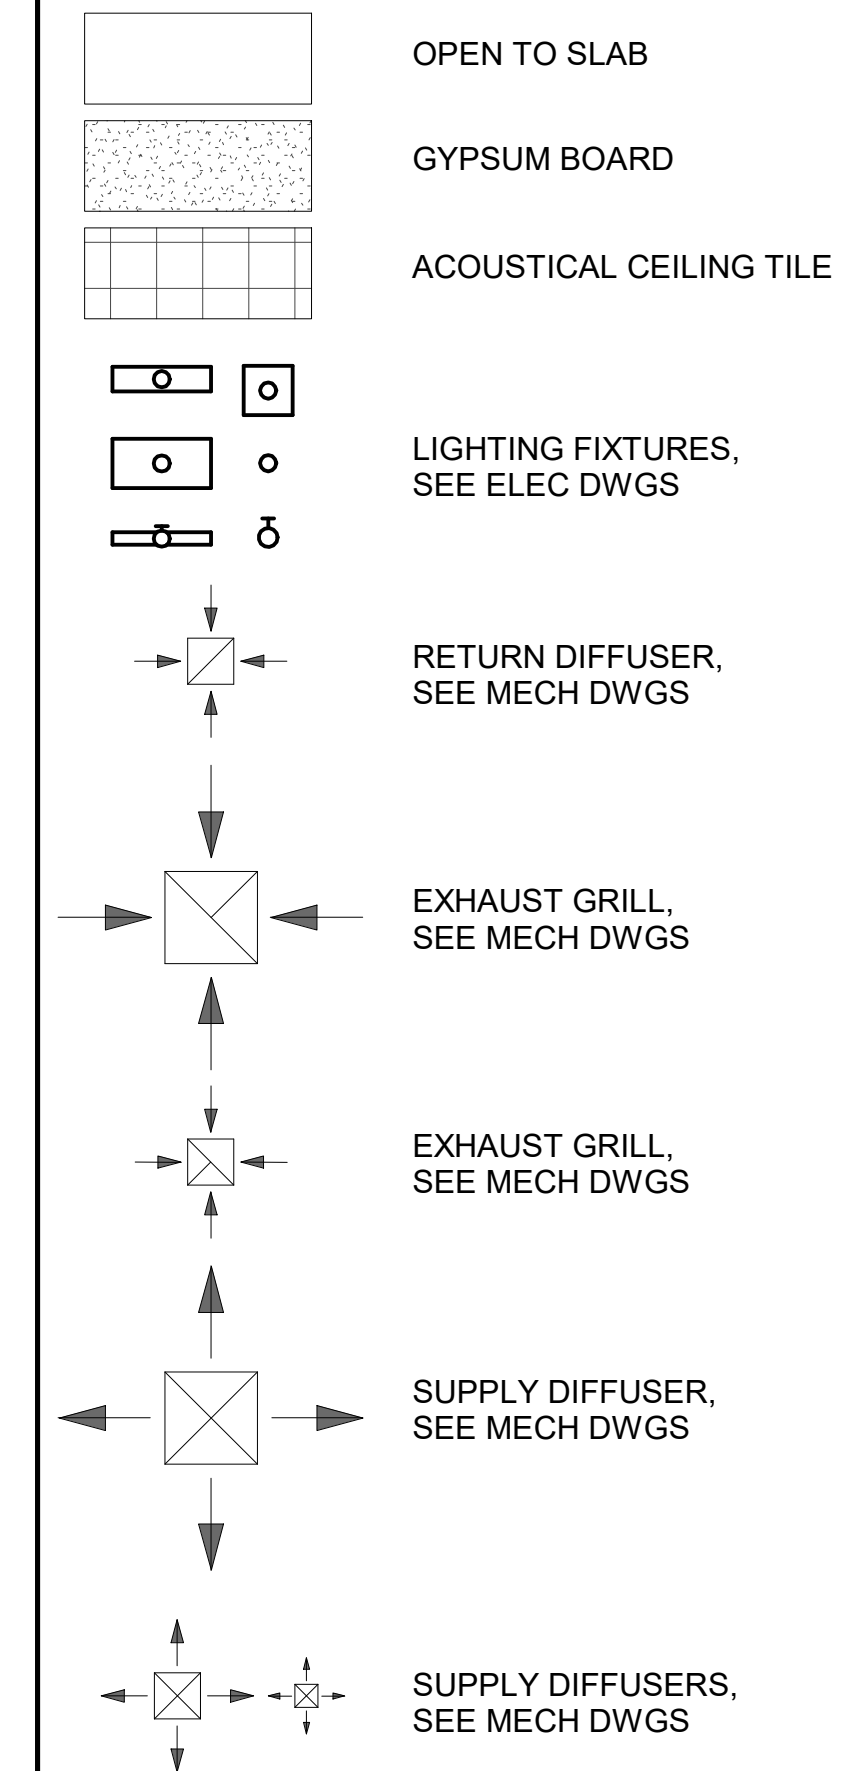

CLIN 0001

KEY PLAN

VMS - LEVEL 2
N.T.S.

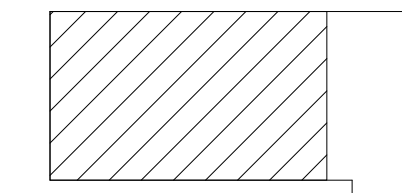


GRAPHIC SCALE



SCALE: 1 : 100

ALL DIMENSIONS AND/OR DIMENSIONS SHOWN IN
CALLOUT/ NOTES ARE IN MILLIMETERS UNLESS
OTHERWISE NOTED.

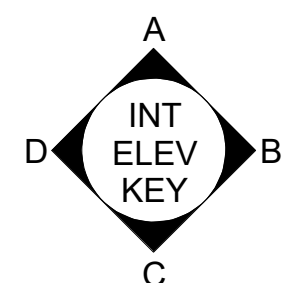

APD AP 96345-5010
FYZO MCA PN7833 VEHICLE MAINTENANCE SHOP


SHEET ID

A-A133

INTERMEDIATE DESIGN

Plot Date: 12/17/2025 5:19:10 AM


Autodesk Docs://SSFM JED IDC VEHICLE MAINTENANCE SHOP/511758_TEMF_ARCH_v2022.rvt

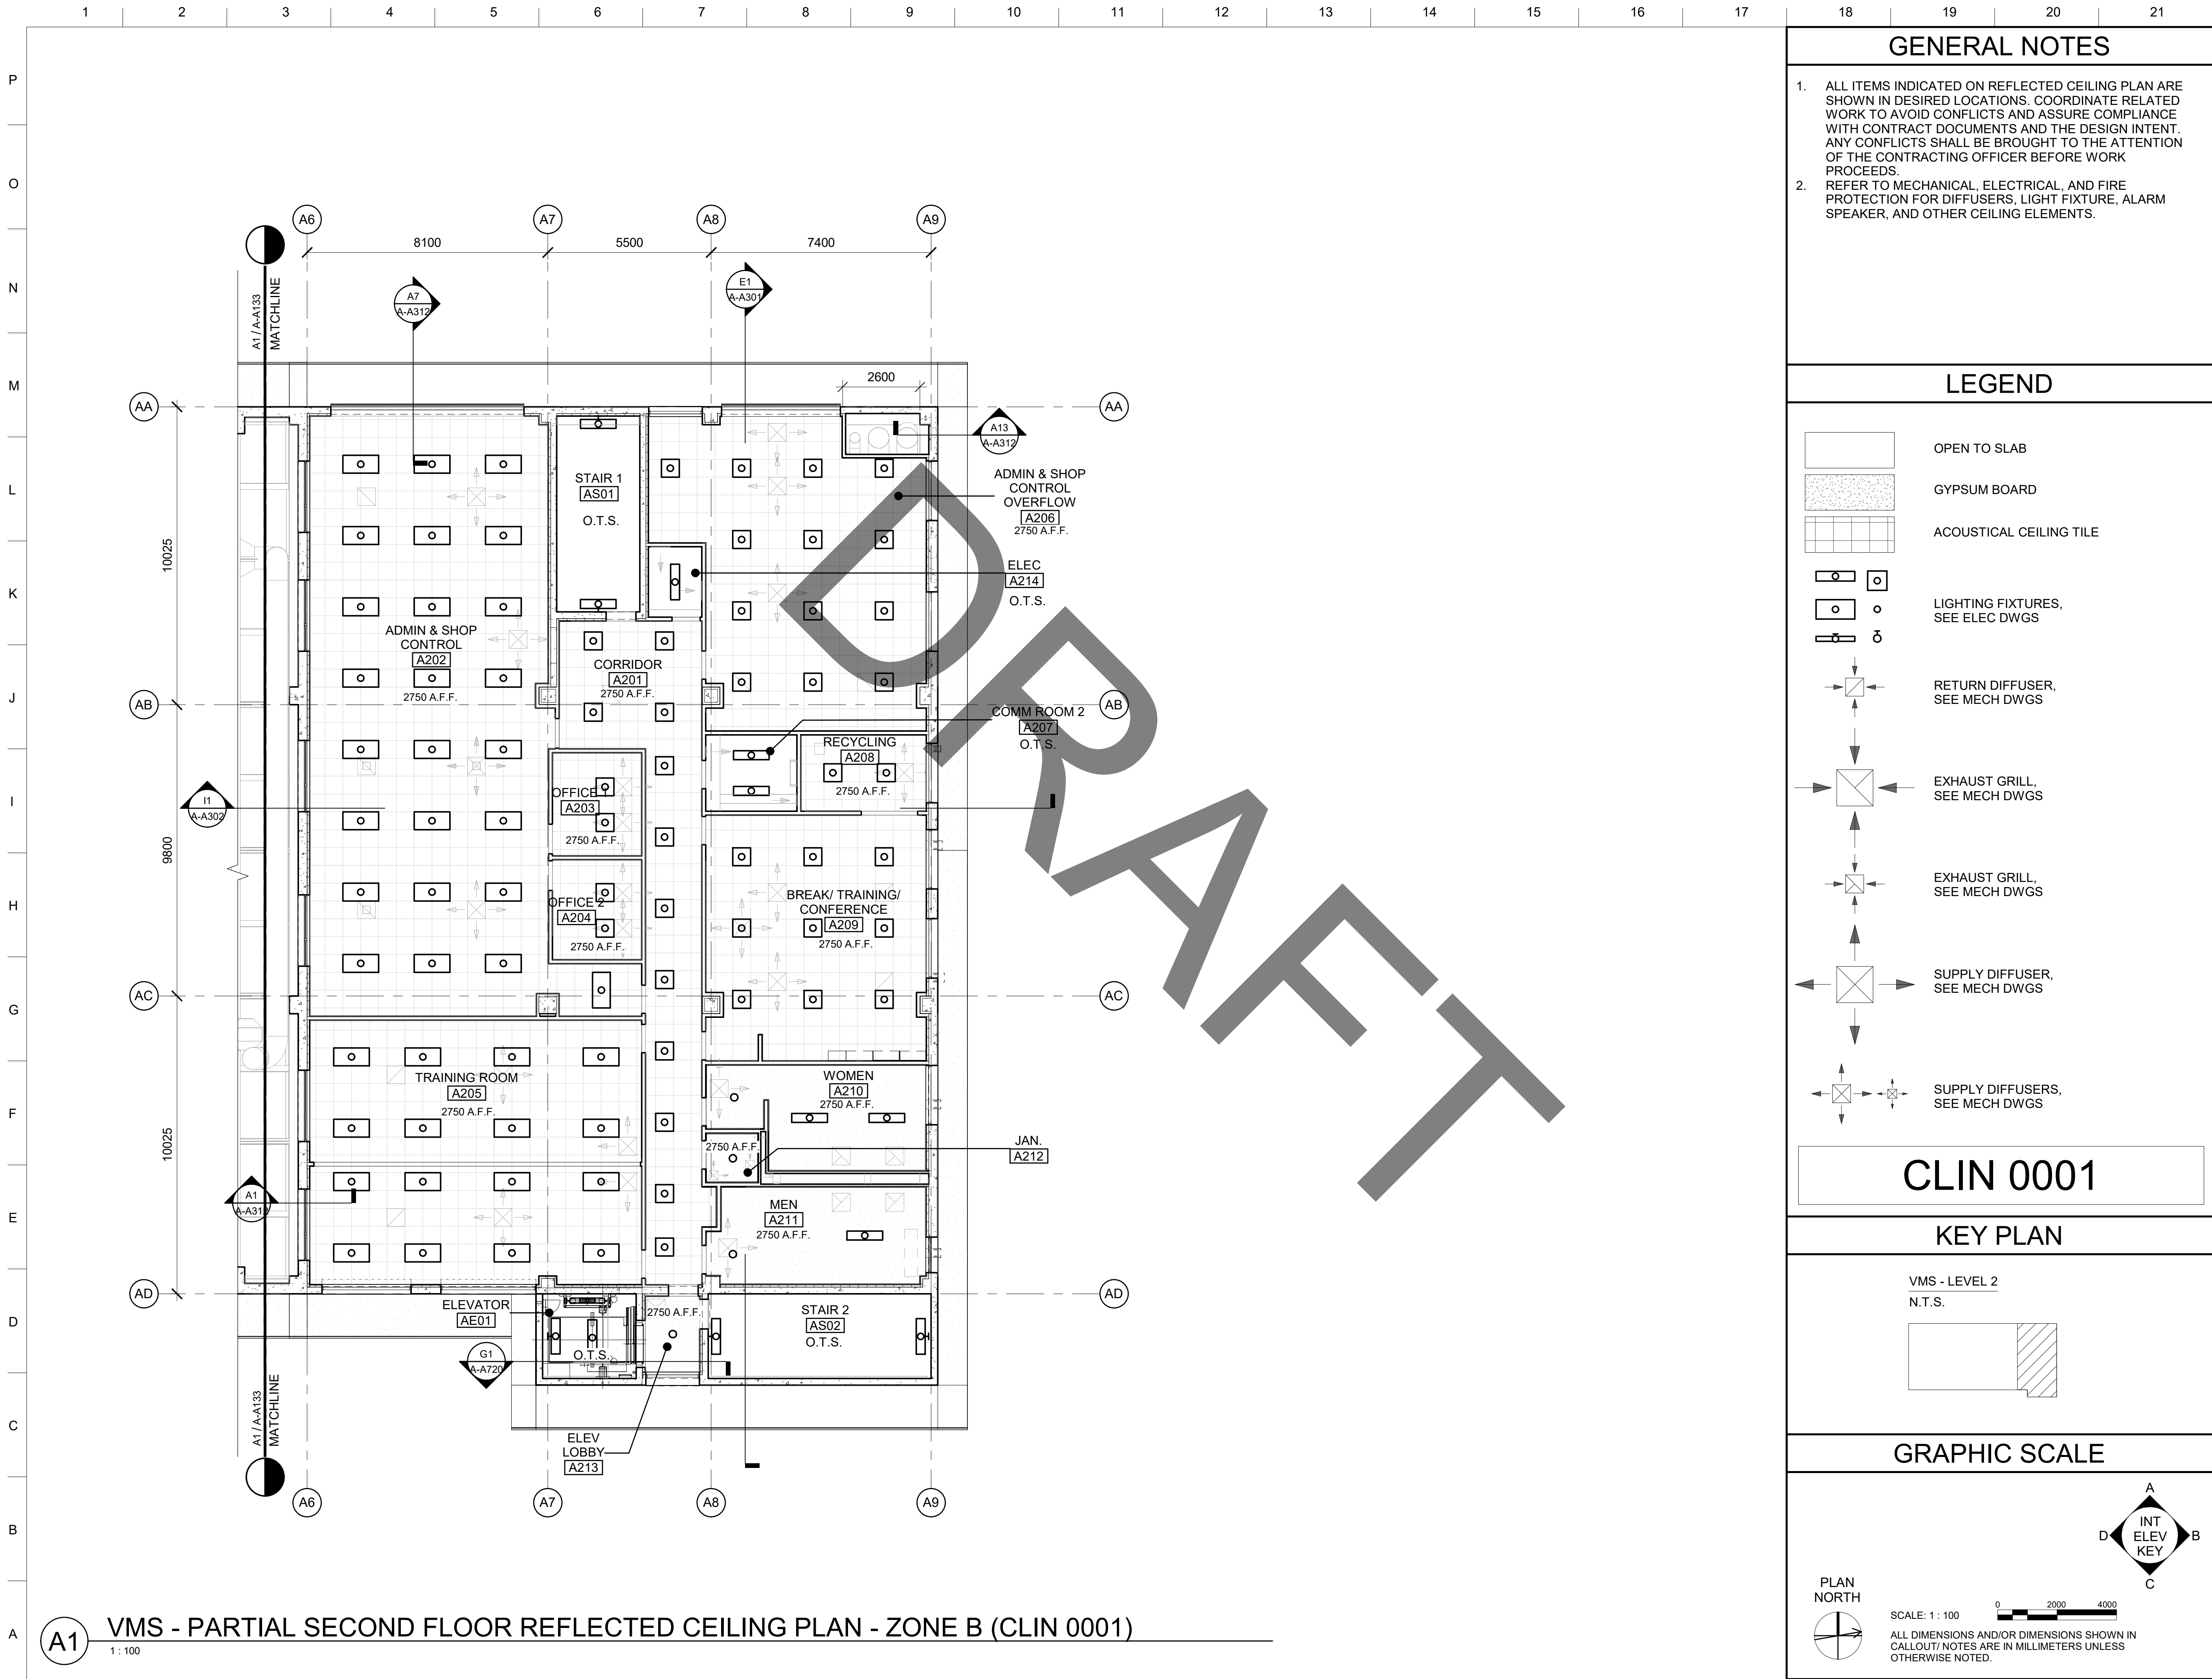


A1 VMS - PARTIAL SECOND FLOOR REFLECTED CEILING PLAN - ZONE B (CLIN 0001)

1 : 100



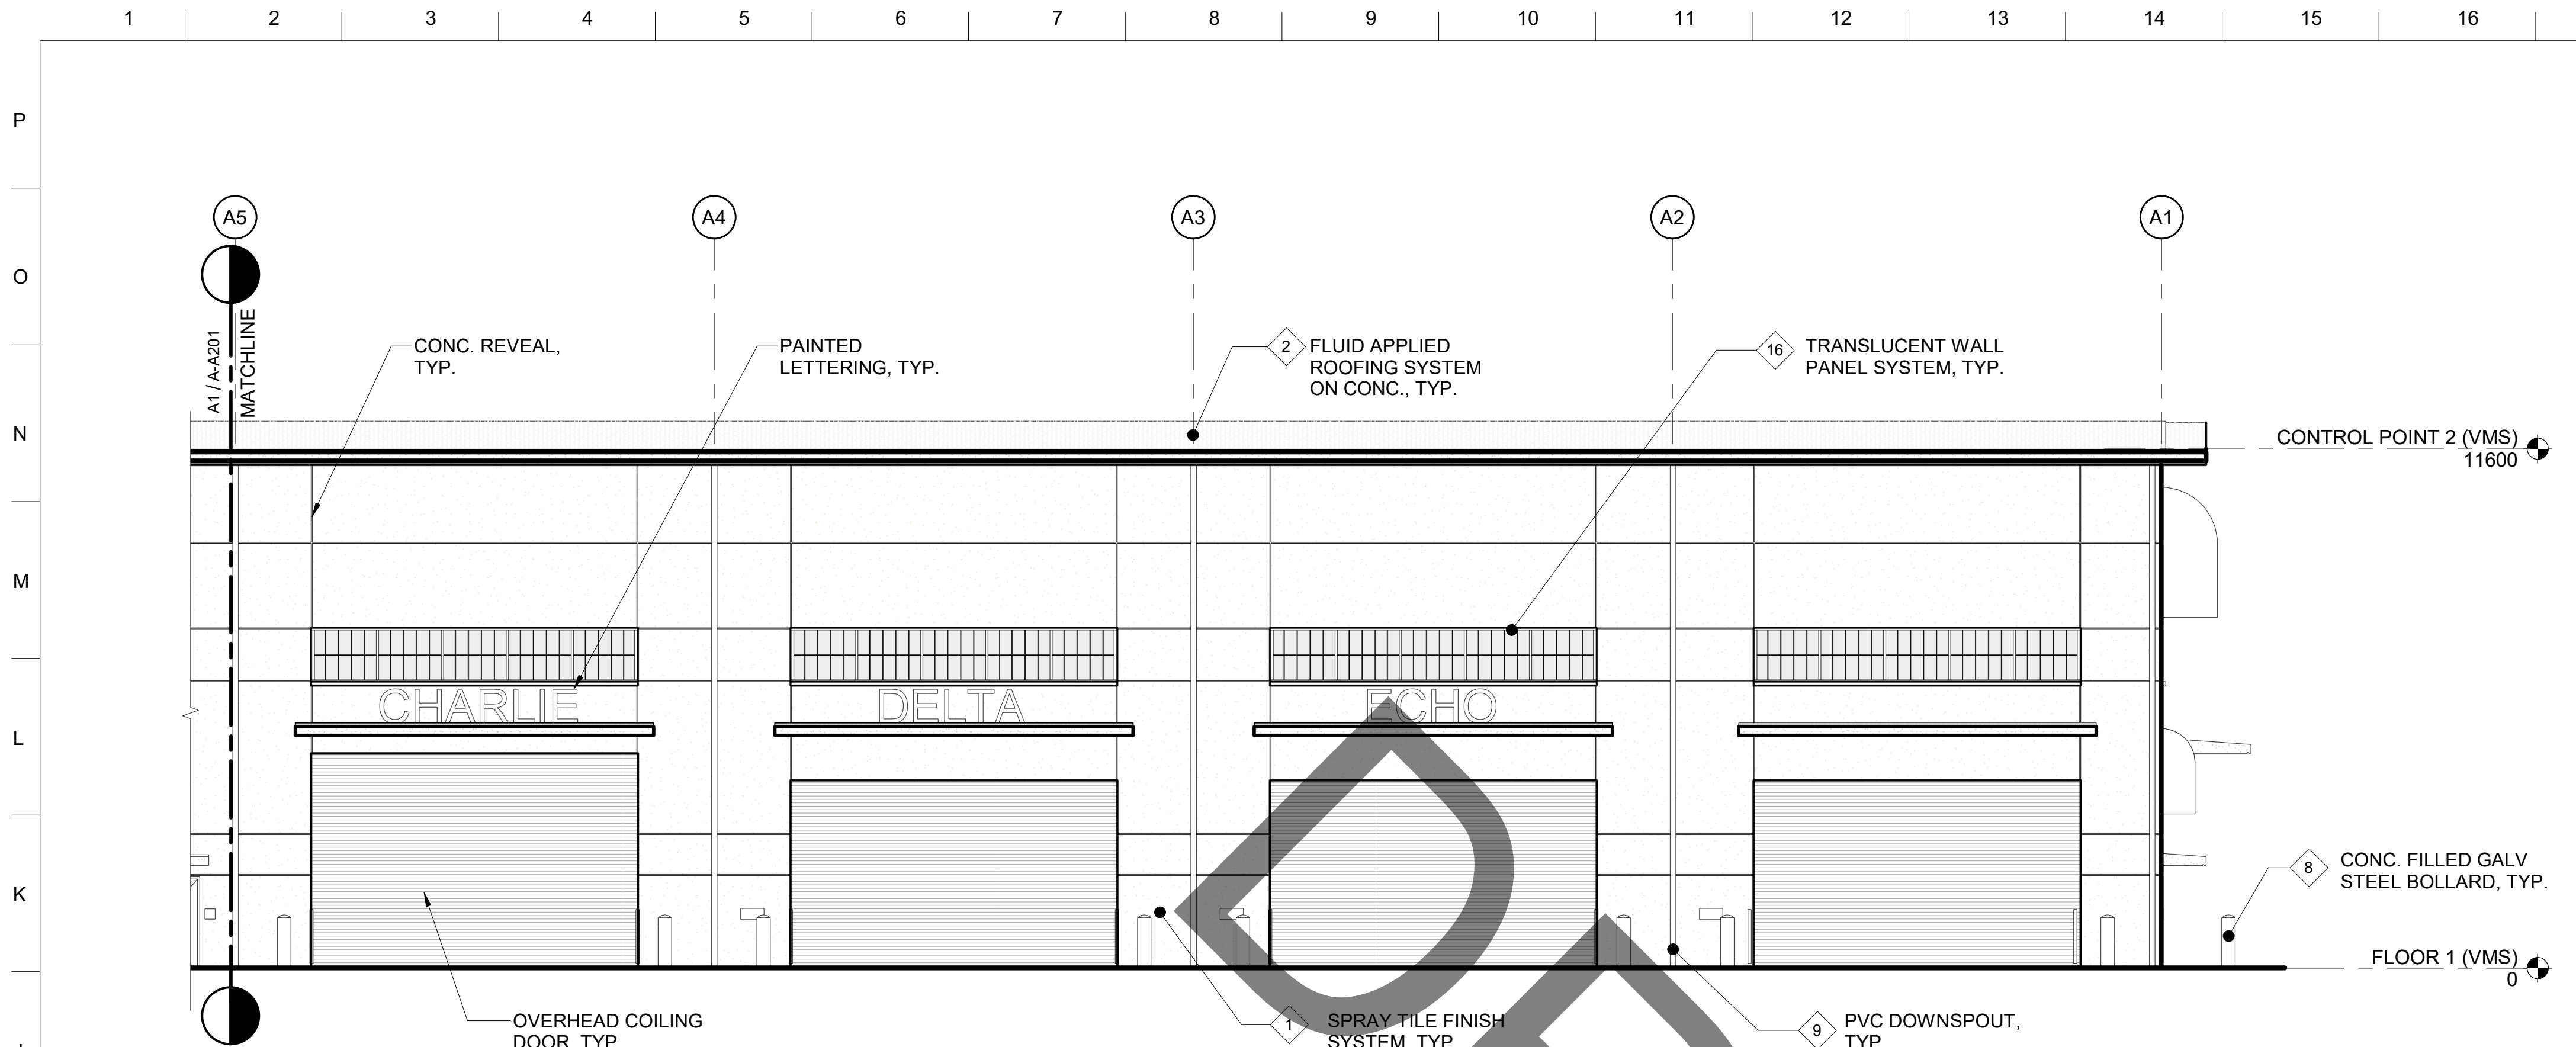

I1 VMS - EXTERIOR ELEVATION - NORTH B (CLIN 0001)
1 : 100

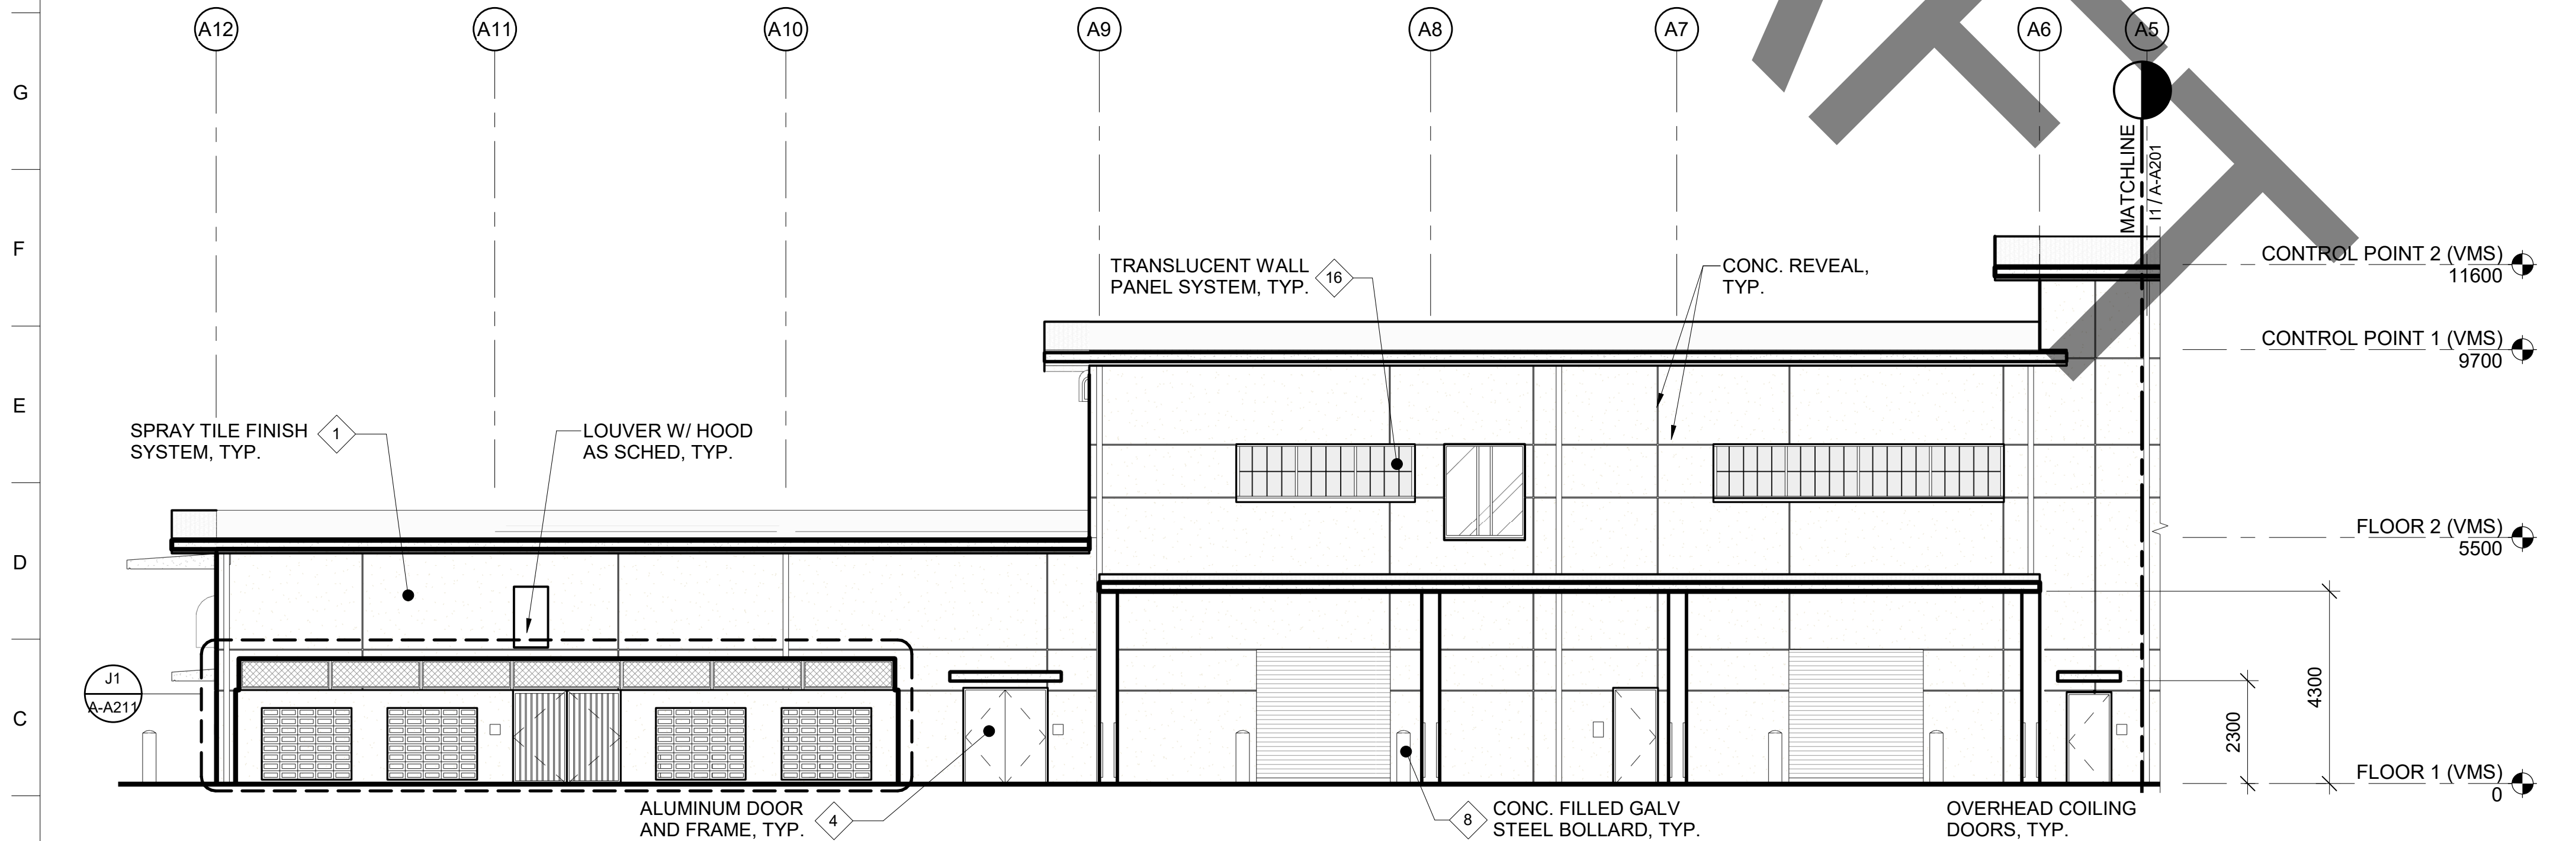

A1 VMS - EXTERIOR ELEVATION - NORTH A (CLIN 0001)
1 : 100

GENERAL NOTES

- SEE SHEET A-200 FOR EXTERIOR FINISH SCHEDULE
- ALL DOWNSPOUTS SHALL BE PROVIDED WITH BOOTS 1200MM HIGH WITH AIR GAP AND CLEANOUTS. ALL DOWNSPOUTS SHALL BE CONNECTED TO THE DRAINAGE SYSTEM. REFER TO CIVIL DRAWINGS.
- CONTRACTOR OR RESPONSIBLE PARTY TO FIELD VERIFY AND CONFIRM ALL DIMENSIONS AND LAYOUT INFORMATION. NOTIFY DESIGNER OF ANY CONFLICTS OR DISCREPENCIES PRIOR TO CONSTRUCTION.
- DO NOT SCALE DRAWINGS.
- DIMENSIONS MARKED "CLR" ARE FROM FINISH SURFACE TO FINISH SURFACE
- SEE STRUCTURAL DRAWINGS FOR CONCRTE WALL THICKNESSES



US Army Corps
of Engineers ®

DATE	DESCRIPTION	MARK

DESIGNED BY: KELLYWOOD	ISSUE DATE:
DRAWN BY: J. MANUJA	SOLICITATION NO.:
CHECKED BY:	CONTRACT NO.:
SUBMITTED BY:	W72WY-17-D-0003
SIZE: ANSI D	

US ARMY CORPS OF ENGINEERS JAPAN ENGINEER DISTRICT OKINAWA AREA OFFICE APO AP 96343-5132	DESIGN PARTNERS INCORPORATED 1580 MAKALOA STREET, SUITE 1100 HONOLULU, HAWAII 96814
---	---

APO AP 96343-50110 FY20 MCA PN7833 VEHICLE MAINTENANCE SHOP	VMS - EXTERIOR ELEVATIONS (CLIN 0001)
--	---------------------------------------

SHEET ID


A-A201

CLIN 0001


GRAPHIC SCALE

SCALE: 1 : 100
0 2000 4000

ALL DIMENSIONS AND/OR DIMENSIONS SHOWN IN
CALLOUT/ NOTES ARE IN MILLIMETERS UNLESS
OTHERWISE NOTED.

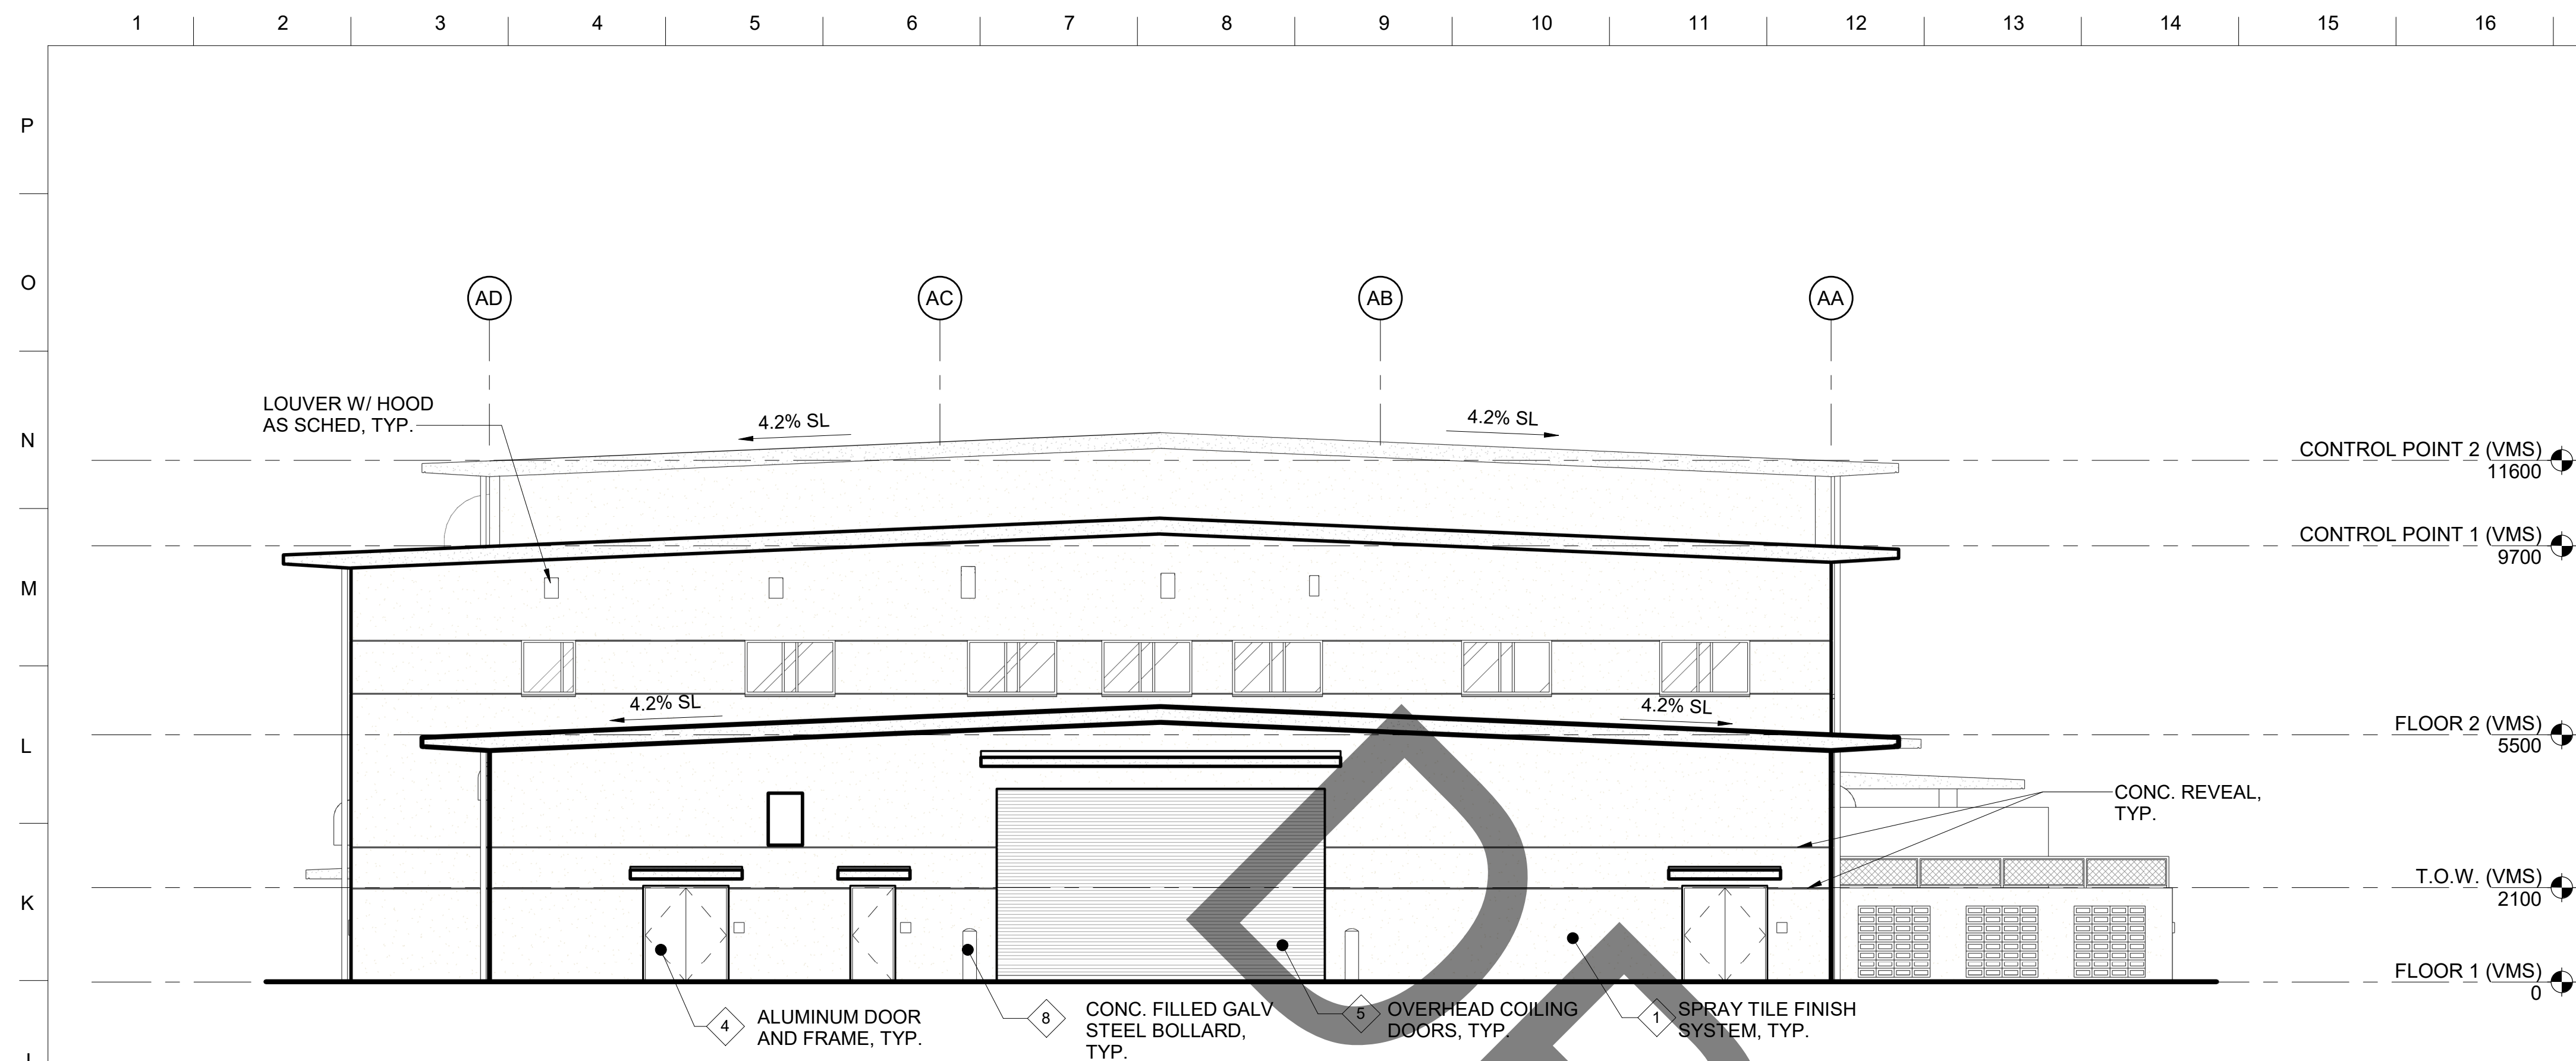

11 VMS - EXTERIOR ELEVATION - EAST (CLIN 0001)
1:100

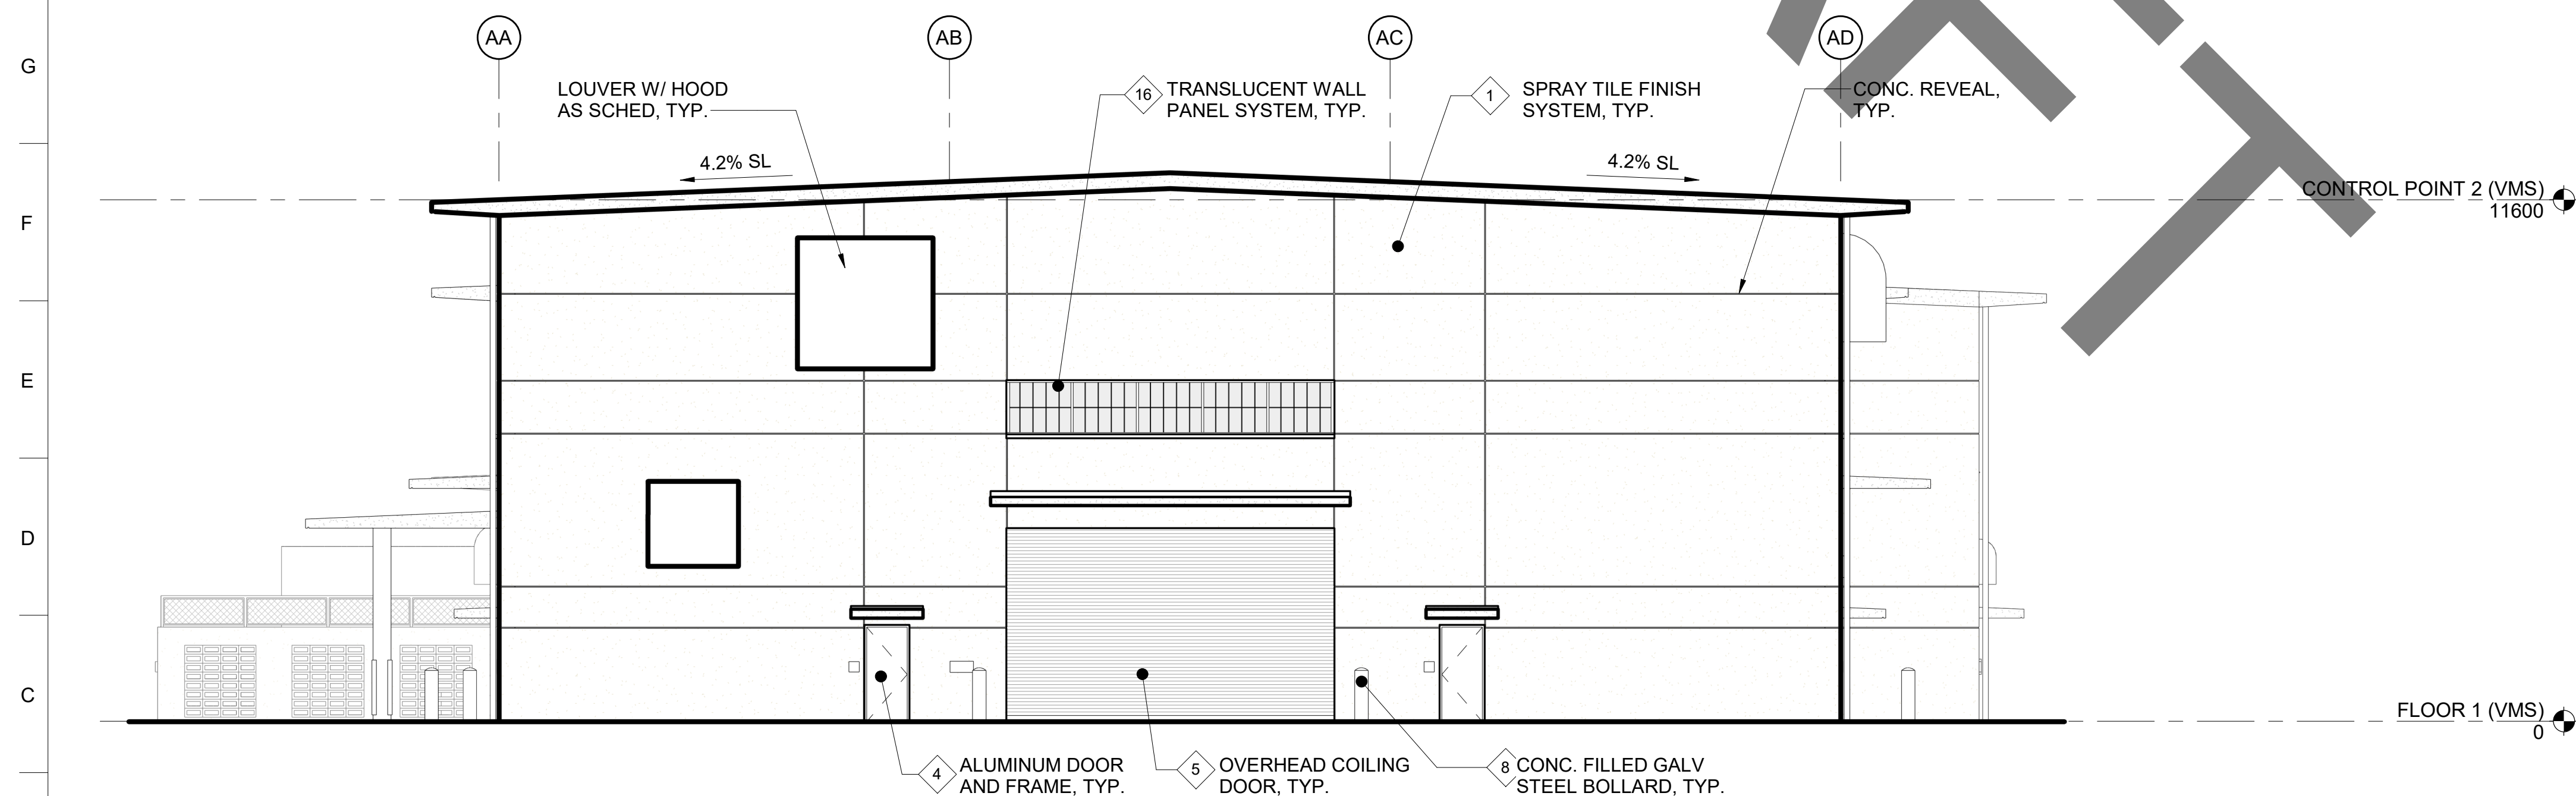

A1 VMS - EXTERIOR ELEVATION - WEST (CLIN 0001)
1:100

GENERAL NOTES

1. SEE SHEET A-200 FOR EXTERIOR FINISH SCHEDULE
2. ALL DOWNSPOUTS SHALL BE PROVIDED WITH BOOTS 1200MM HIGH WITH AIR GAP AND CLEANOUTS. ALL DOWNSPOUTS SHALL BE CONNECTED TO THE DRAINAGE SYSTEM. REFER TO CIVIL DRAWINGS.
3. CONTRACTOR OR RESPONSIBLE PARTY TO FIELD VERIFY AND CONFIRM ALL DIMENSIONS AND LAYOUT INFORMATION. NOTIFY DESIGNER OF ANY CONFLICTS OR DISCREPENCIES PRIOR TO CONSTRUCTION.
4. DO NOT SCALE DRAWINGS.
5. DIMENSIONS MARKED "CLR" ARE FROM FINISH SURFACE TO FINISH SURFACE
6. SEE STRUCTURAL DRAWINGS FOR CONCRTE WALL THICKNESSES



US Army Corps
of Engineers ®

[illegible]

US ARMY CORPS OF ENGINEERS ARMY ENGINEER DISTRICT OFFICE APO AP 96374-5132	ISSUE DATE:
DESIGN PARTNERS INCORPORATED 1580 KAHALA DRIVE, SUITE 1100 HONOLULU, HAWAII 96814	SOLICITATION NO.: DRAWN BY: KELLINGWOOD IROLLO, J MANUUA CHECKED BY: DIMITROV SUBMITTED BY: CONTRACT NO.: W812EN-17D-0083 DATE:
	SIZE: ☐ A ☐ D

833 VEHICLE MAINTENANCE SHOP

VMS - EXTERIOR ELEVATIONS (CLIN 0001)

SHEET ID

A-A202

CLIN 0001

GRAPHIC SCALE

SCALE: 1 : 100




ALL DIMENSIONS AND/OR DIMENSIONS SHOWN IN
CALLOUT/ NOTES ARE IN MILLIMETERS UNLESS
OTHERWISE NOTED.

Autodesk Docs://SSFM JED IDC VEHICLE MAINTENANCE SHOP/511758_TEMF_ARCH_ARCH_v2022.rvt

Plot Date: 12/17/2025 5:19:29 AM File Path:

INTERMEDIATE DESIGN

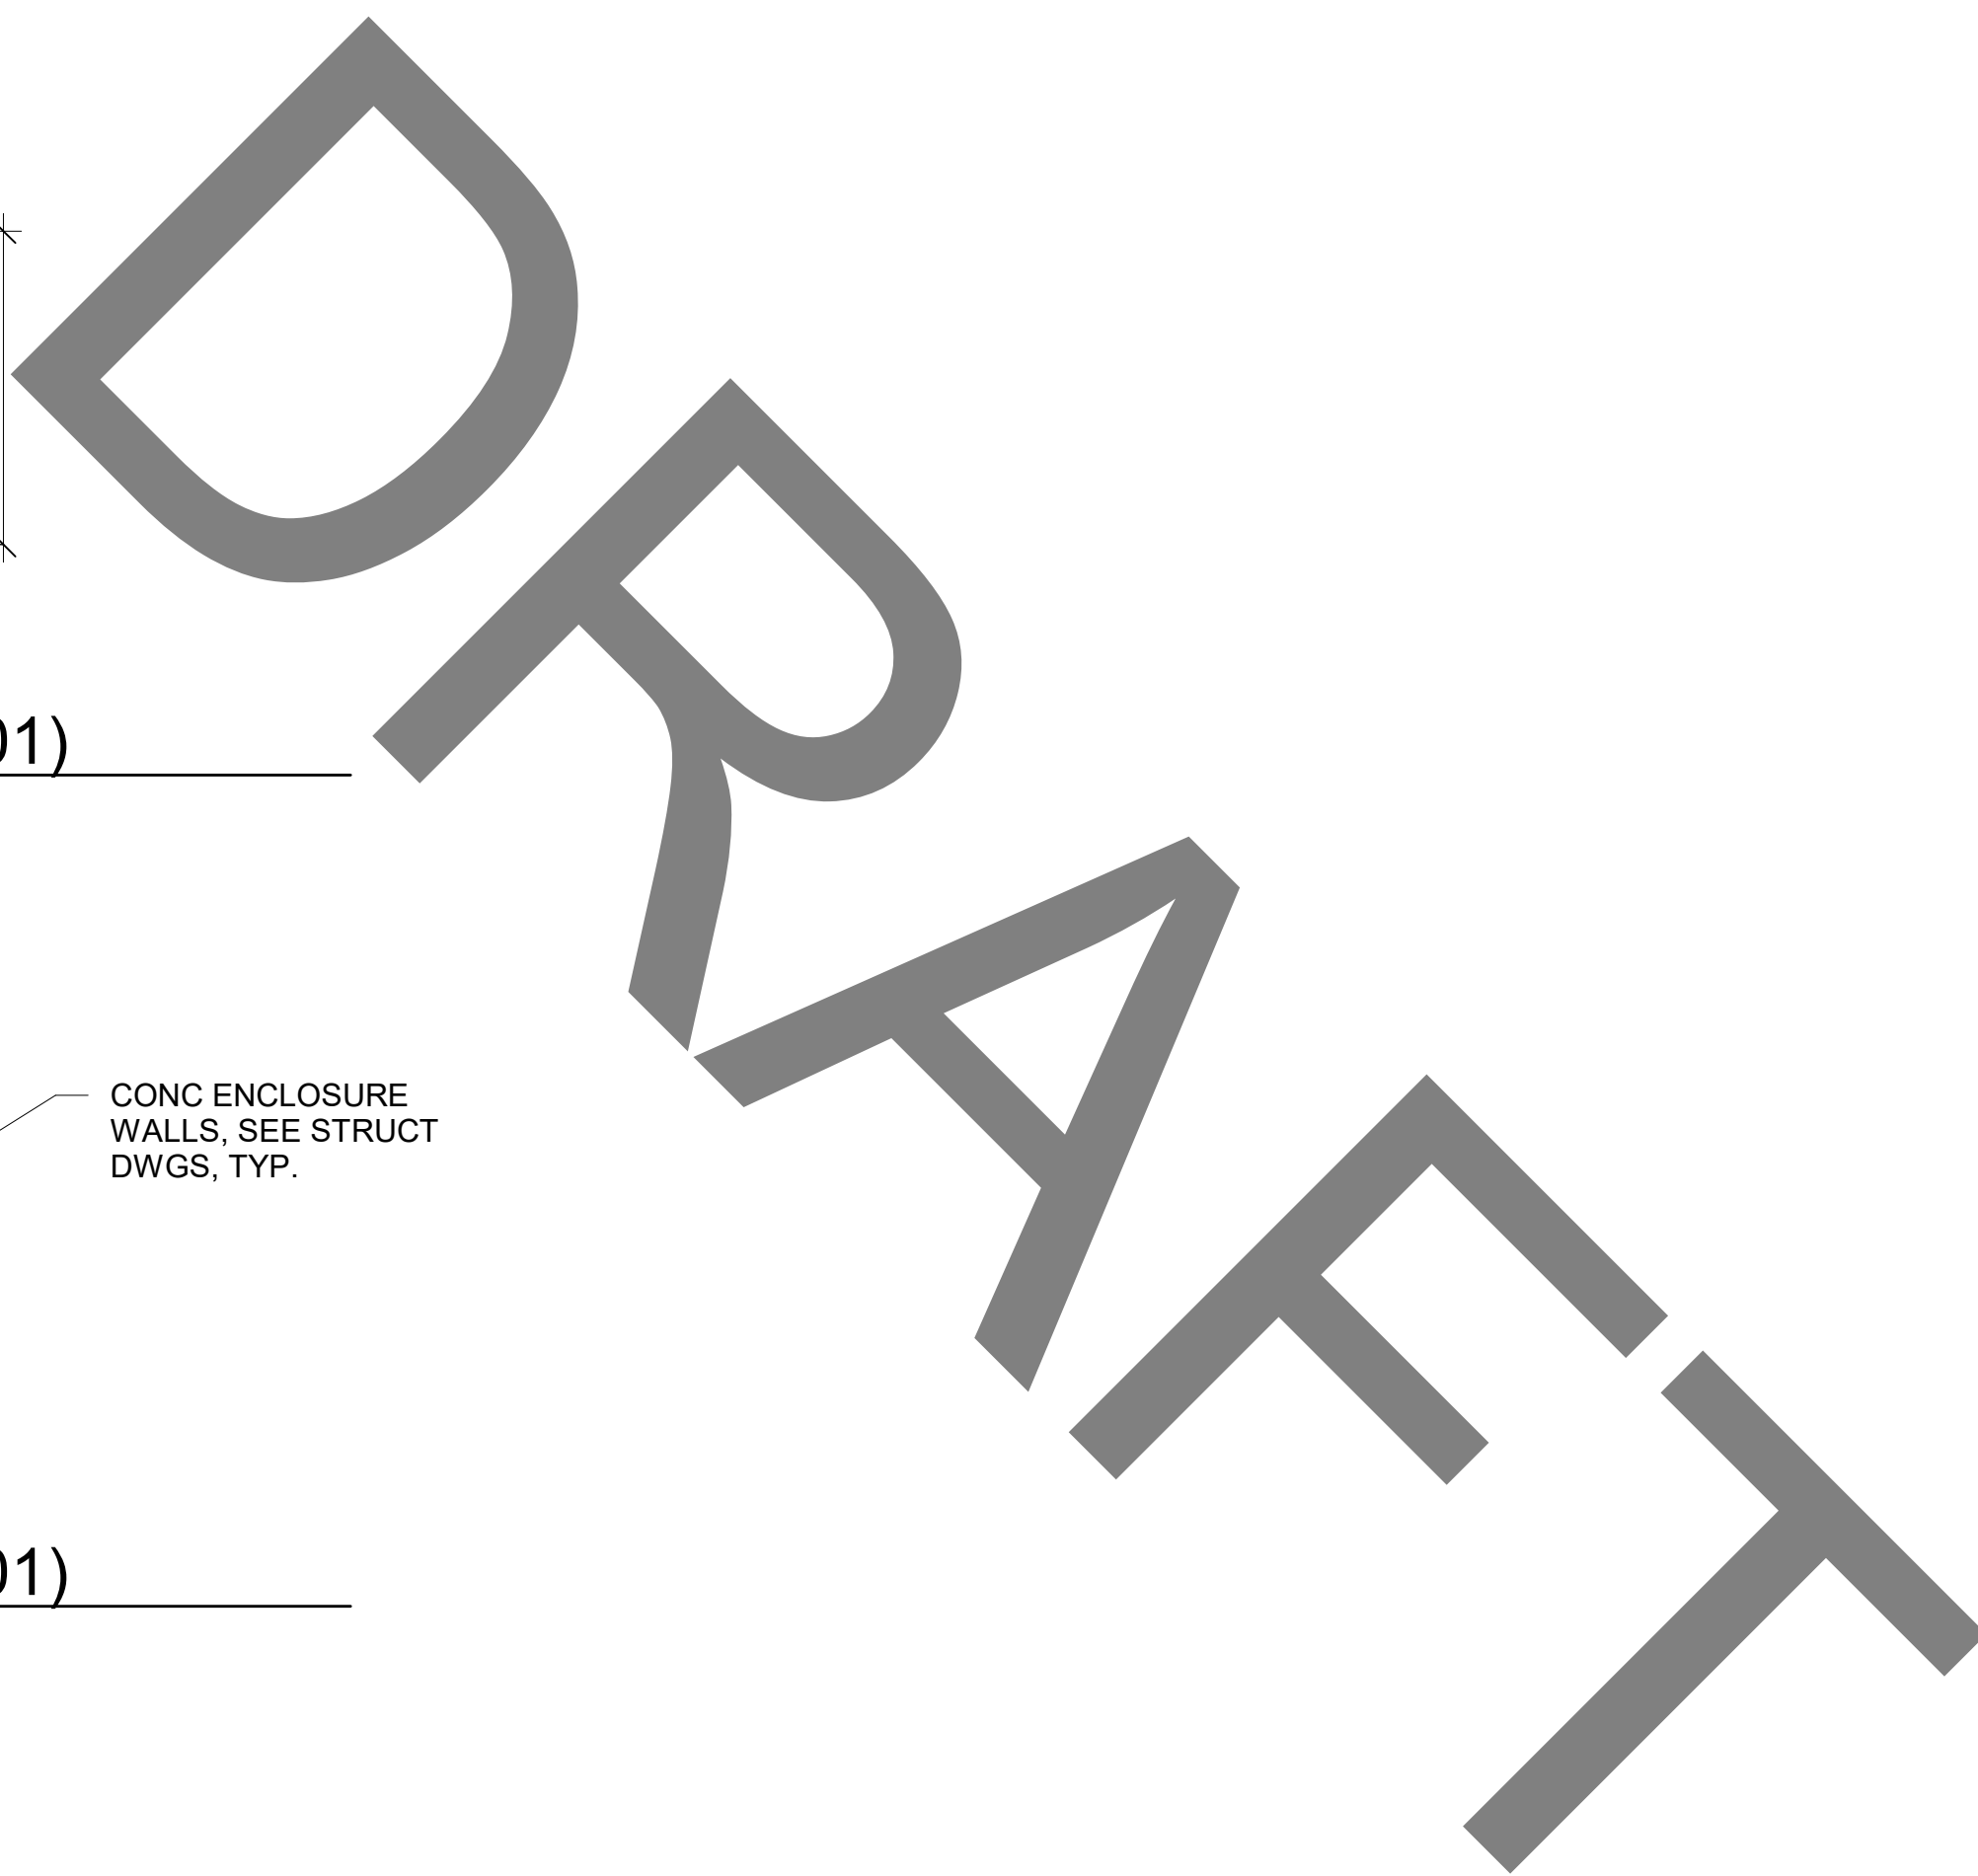


Technical drawing of a building facade. The drawing shows a grid of windows and a decorative top section. The dimensions are indicated as follows:

- Overall width: 1600
- Overall height: 2100
- Height of the decorative top section: 400

The diagram shows a building facade with three windows and three sets of doors. Each window is divided into four panes. Each set of doors consists of four individual doors arranged in a row. An arrow points to the rightmost set of doors.

CONC ENCLOSURE
WALLS, SEE STRUCT
DWGS, TYP.

- CLIN 0001

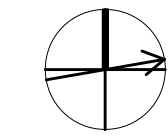

SCALE: 1 : 50

US ARMY CORPS OF ENGINEERS JAPAN ENGINEER DISTRICT OKINAWA AREA OFFICE APO AF 96376-5132	DESIGNED BY: K.ELINGWOOD	ISSUE DATE:
DESIGN PARTNERS INCORPORATED 1350 MAKALOA STREET, SUITE 1100 HONOLULU, HAWAII 96814	DRAWN BY: TROLLO, J. MANUIA	SOLICITATION NO.:
	CHECKED BY: D. MOATS	CONTRACT NO.:
	SUBMITTED BY:	W912N4-17-D-0003
	SIZE:	

SHEET ID

GRAPHIC SCALE


ALL DIMENSIONS AND/OR DIMENSIONS SHOWN IN
CALLOUT/ NOTES ARE IN MILLIMETERS UNLESS
OTHERWISE NOTED.

Autodesk Docs://SSFM JED IDC VEHICLE MAINTENANCE SHOP/511758 TEMF ARCH v2022.mt

File Path:

Plot Date: 12/17/2025 5:10:35 AM

INTERMEDIATE DESIGN

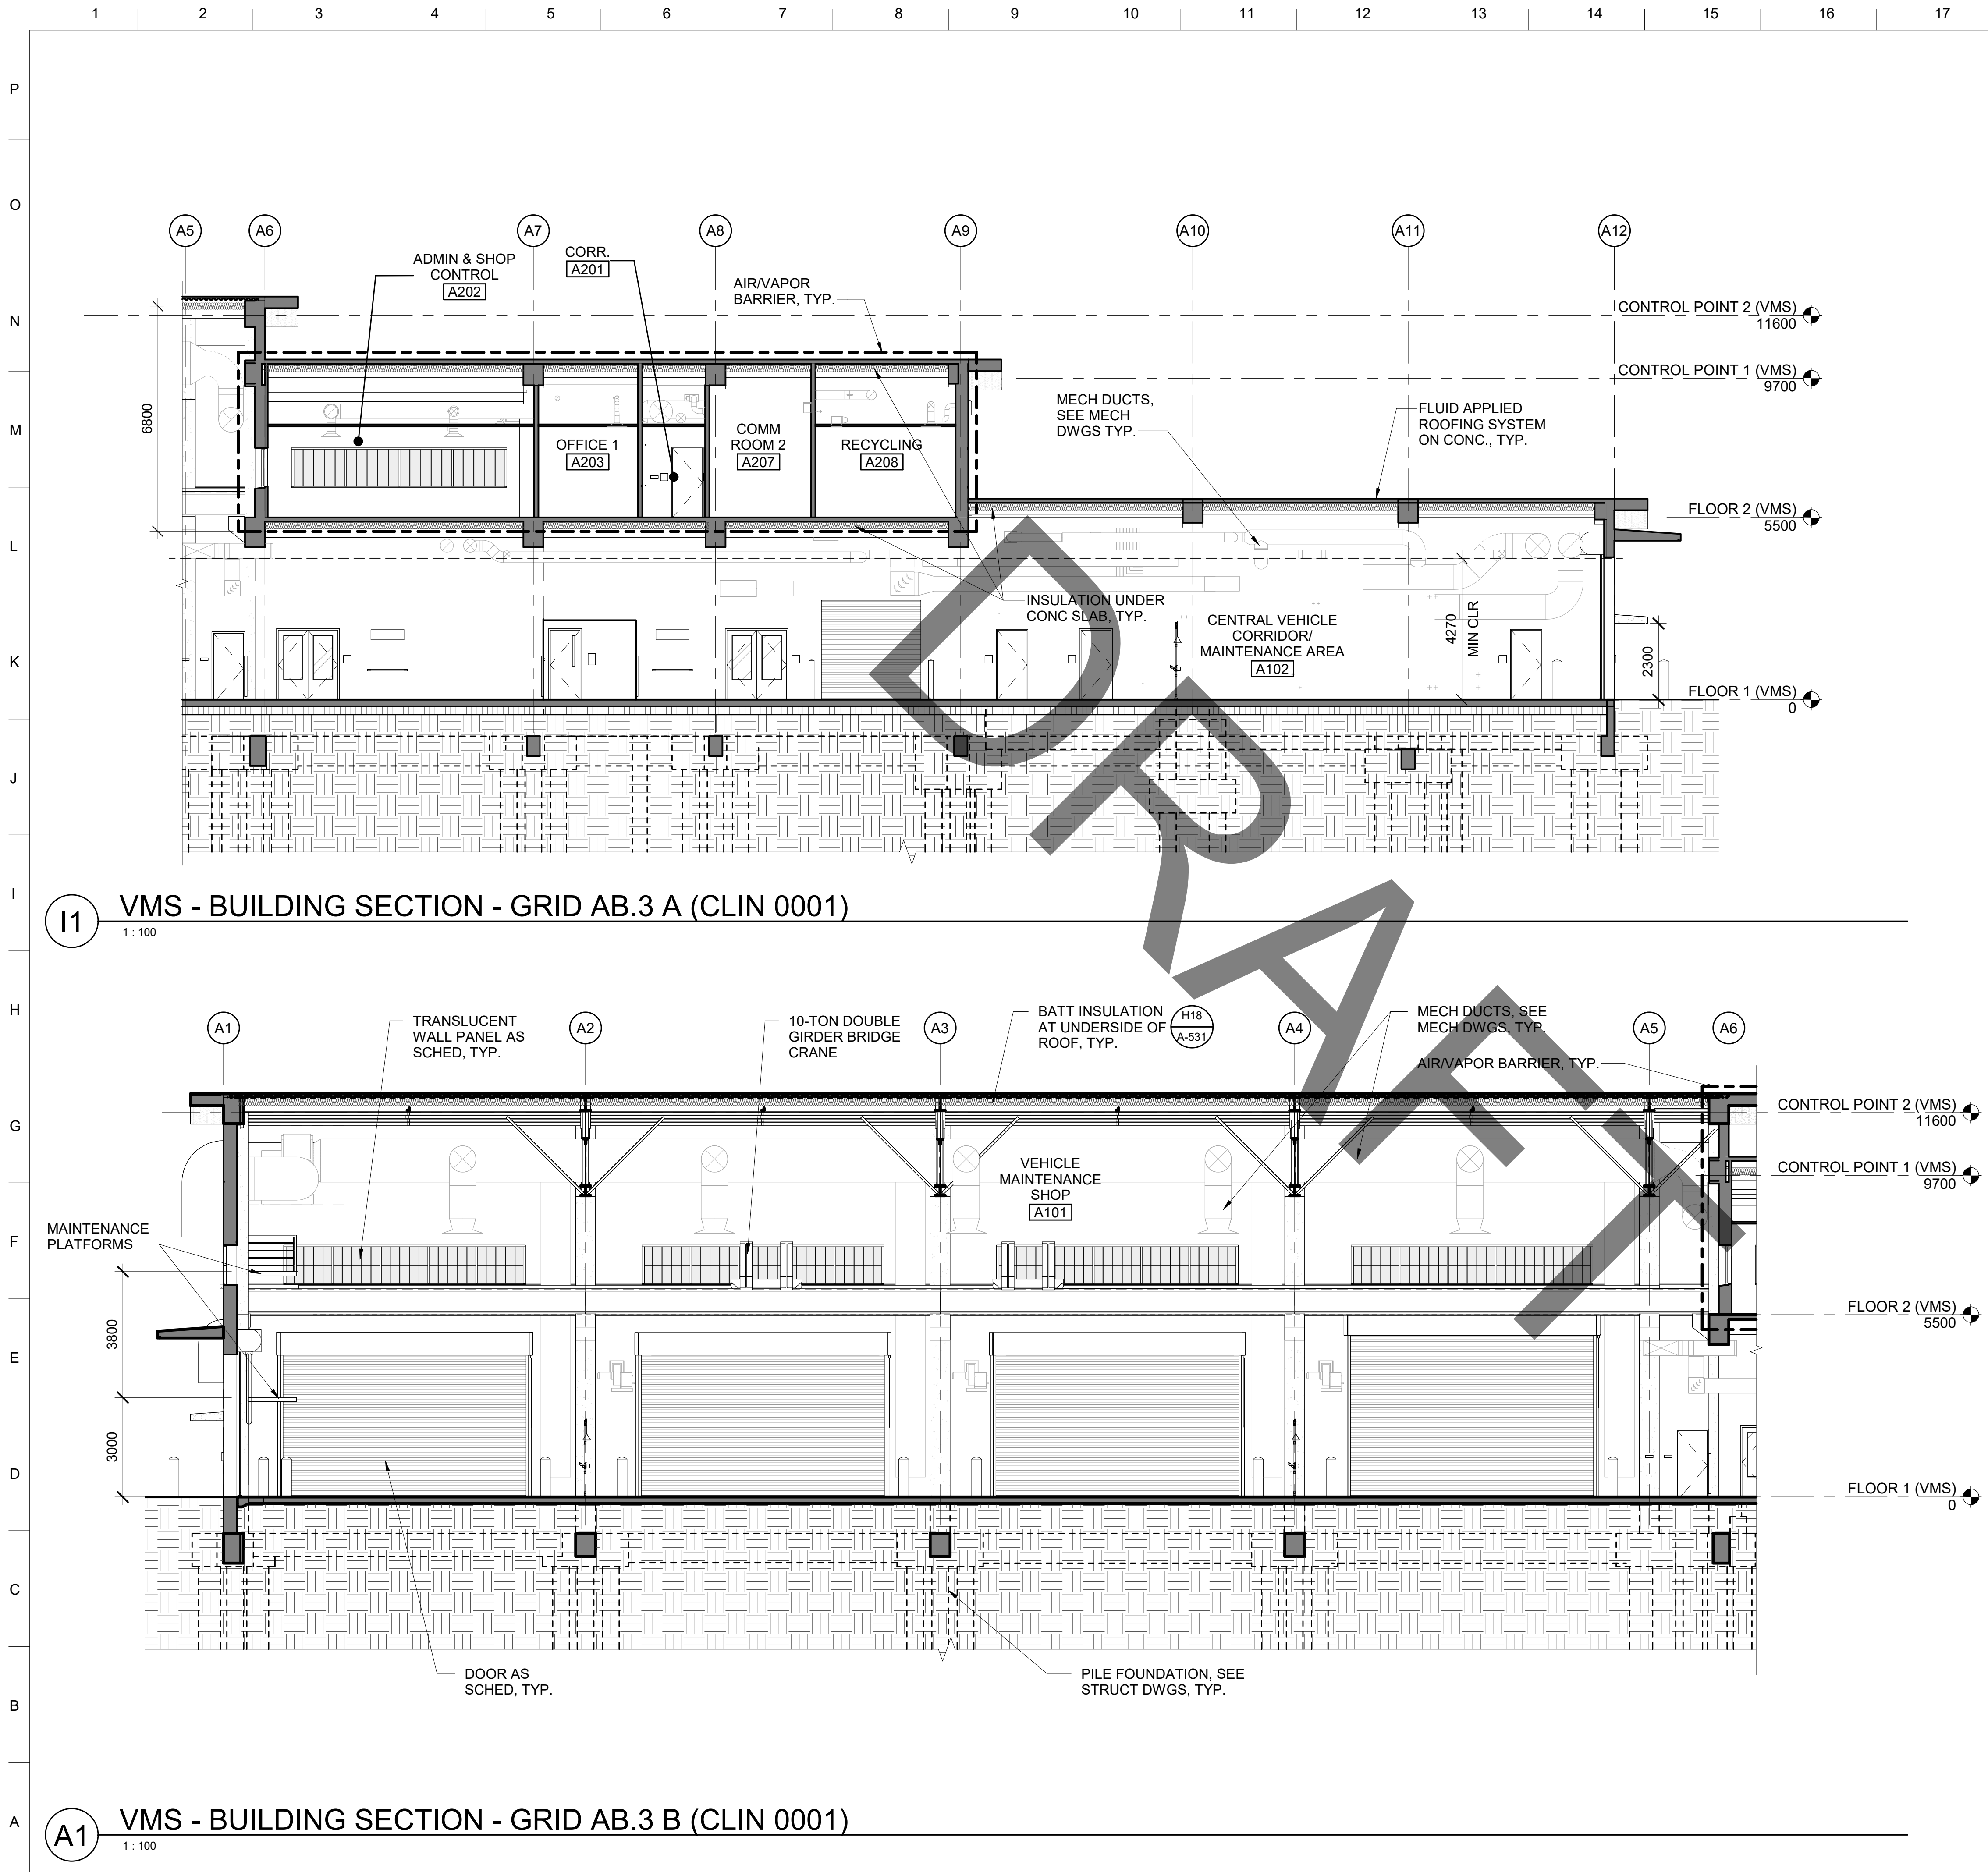

- ### GENERAL NOTES
1. CONTRACTOR OR RESPONSIBLE PARTY TO FIELD VERIFY AND CONFIRM ALL DIMENSIONS AND LAYOUT INFORMATION. NOTIFY DESIGNER OF ANY CONFLICTS OR DISCREPANCIES PRIOR TO CONSTRUCTION.
 2. DO NOT SCALE DRAWINGS.
 3. DIMENSIONS MARKED "CLR" ARE FROM FINISH SURFACE TO FINISH SURFACE.
 4. SEE STRUCTURAL DRAWINGS FOR CONCRETE WALL THICKNESSES.
 5. REFER TO SHEET A-101 TO A-103 FOR AIR BARRIER PLANS.

US Army Corps of Engineers ®	
DATE	
MARK	
DESCRIPTION	

DESIGNED BY: KELLYWOOD	ISSUE DATE:
DRAWN BY: J. MANUJA	SOLICITATION NO.:
CHECKED BY: W. J. MANUJA	CONTRACT NO.:
SUBMITTED BY:	W. J. MANUJA
SIZE: ANSI D	


US ARMY CORPS OF ENGINEERS JAPAN ENGINEER DISTRICT OKINAWA AREA OFFICE APO AP 96376-5132	VMS - BUILDING SECTIONS (CLIN 0001)
DESIGN PARTNERS INCORPORATED 1580 MAKALOA STREET, SUITE 1100 HONOLULU, HAWAII 96814	

CLIN 0001

GRAPHIC SCALE

SCALE: 1 : 100
0 2000 4000
ALL DIMENSIONS AND/OR DIMENSIONS SHOWN IN
CALLOUT/ NOTES ARE IN MILLIMETERS UNLESS
OTHERWISE NOTED.

SHEET ID
A-A302

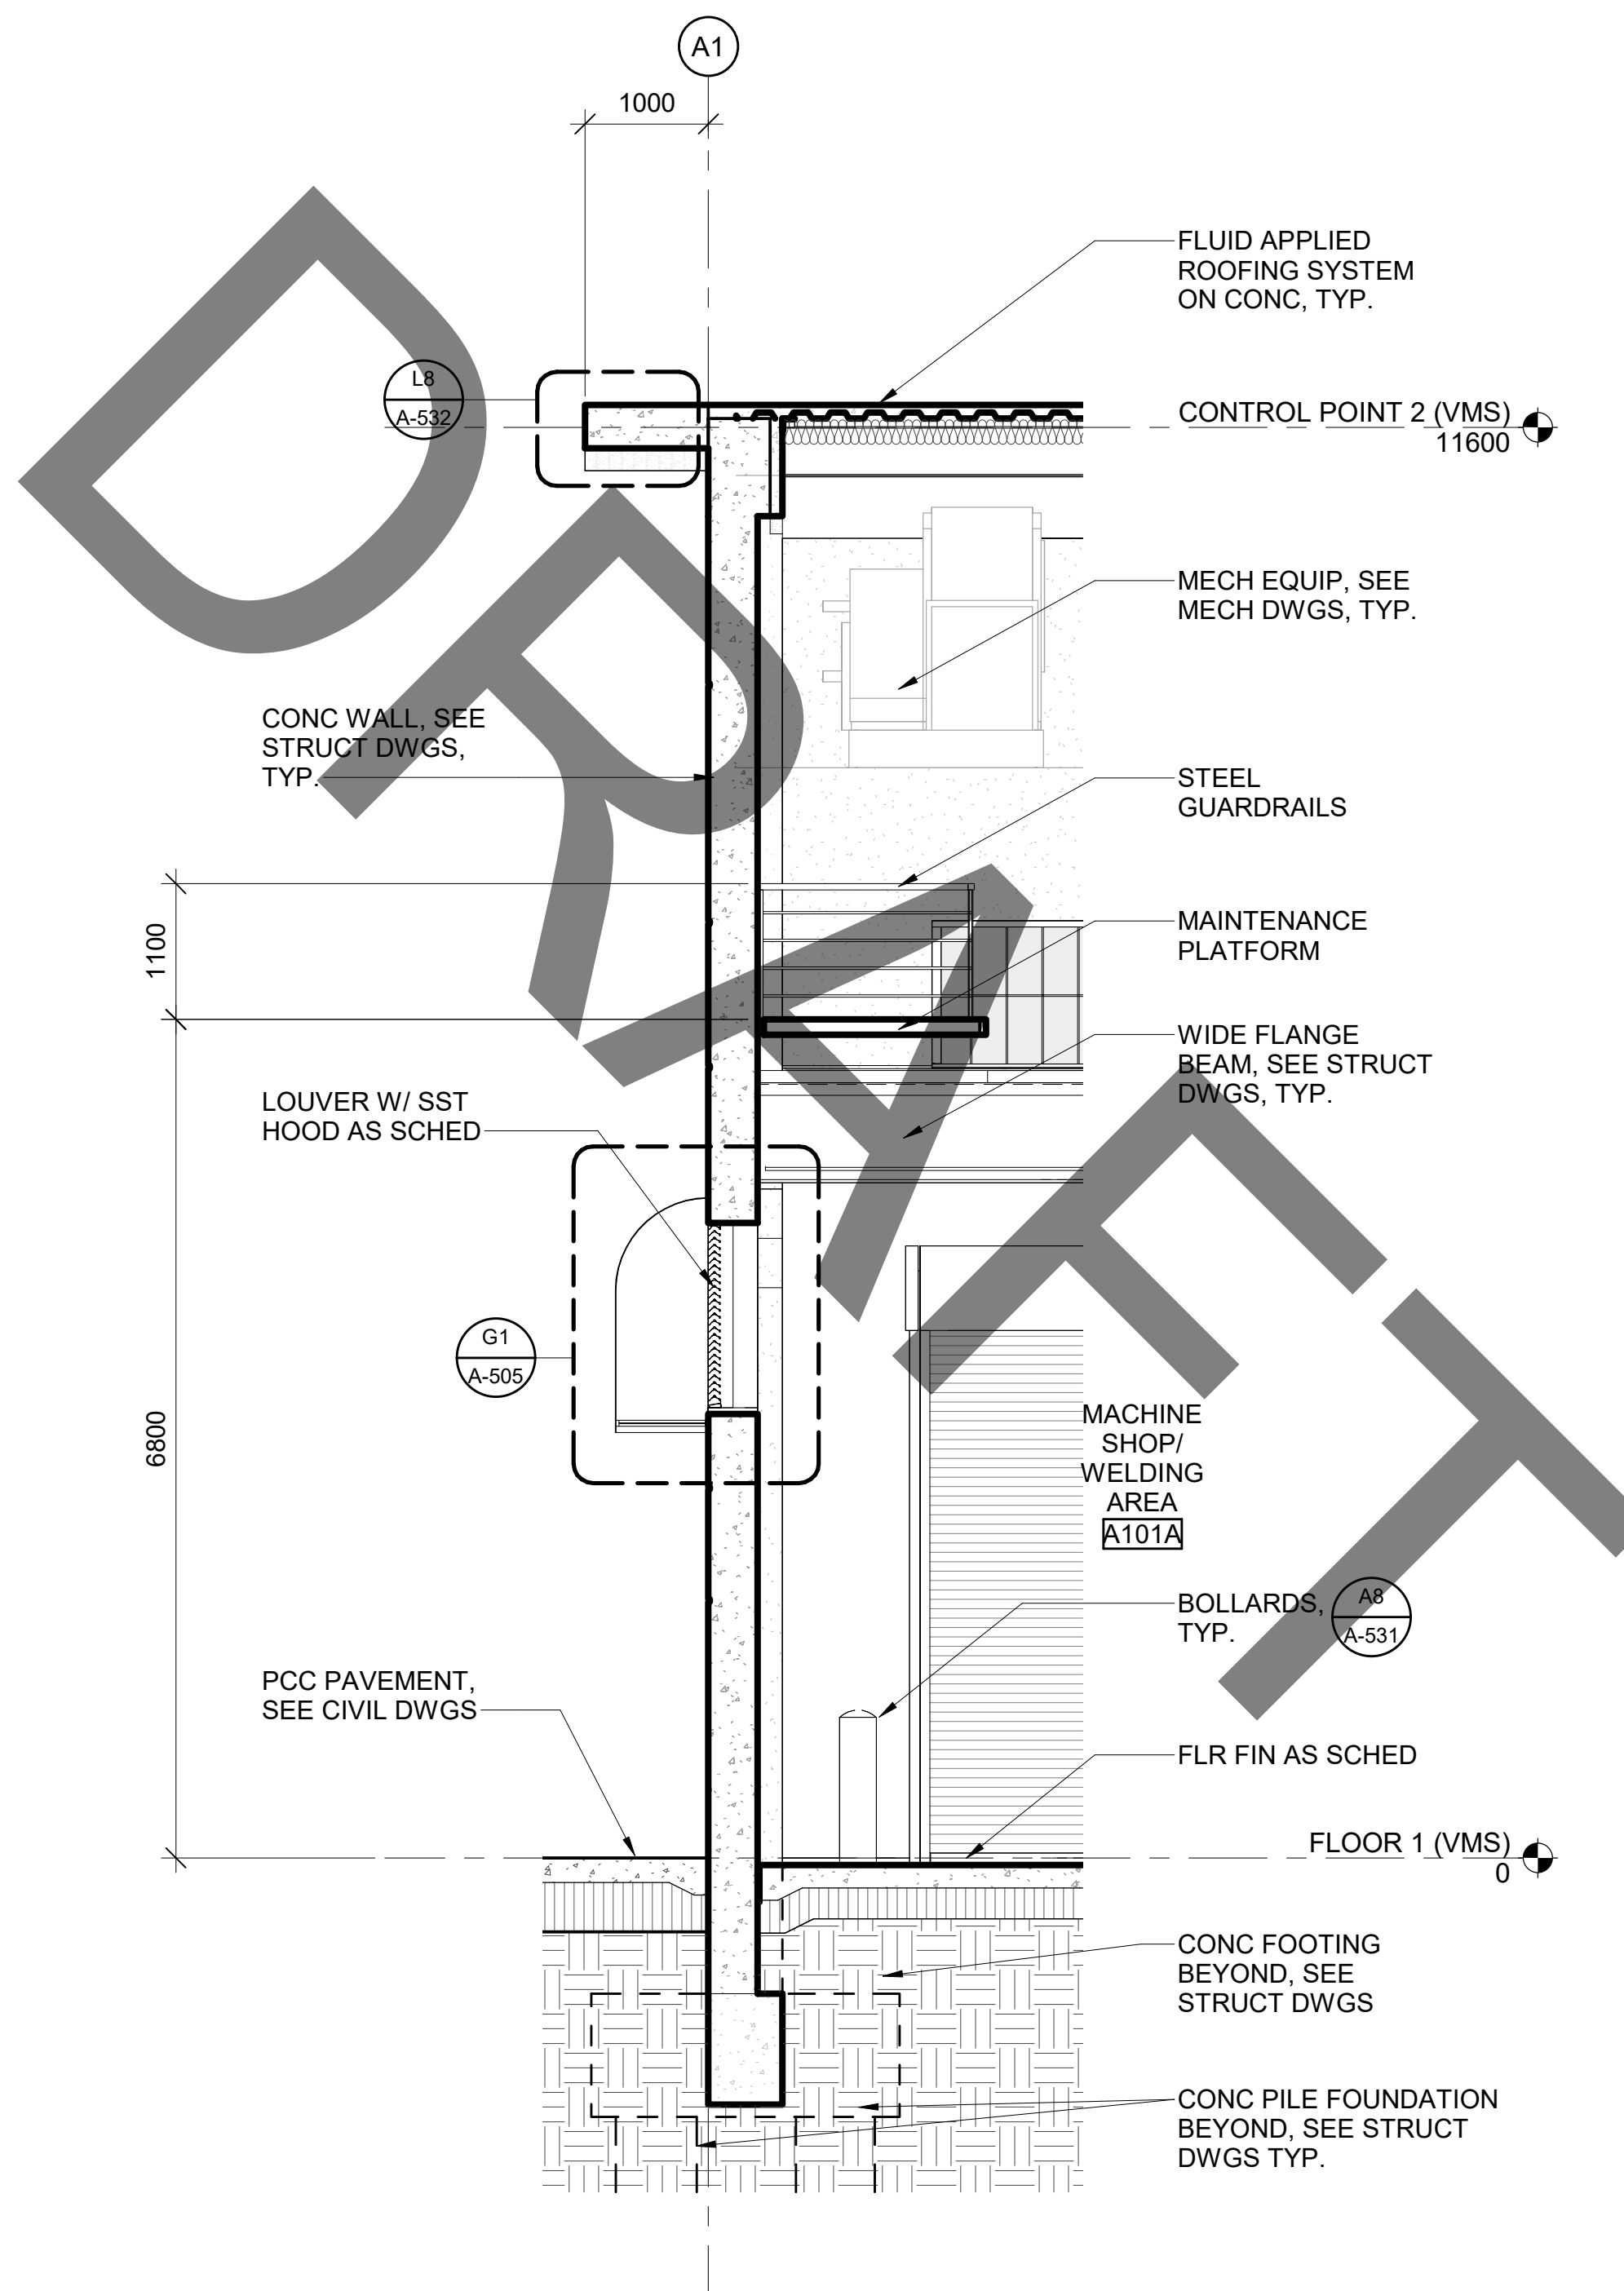

A9 VMS - WALL SECTION 2 (CLIN 0001)
1 : 50

US Army Corps
of Engineers ®

1. CONTRACTOR OR RESPONSIBLE PARTY TO FIELD VERIFY, AND CONFIRM ALL DIMENSIONS AND LAYOUT INFORMATION. NOTIFY DESIGNER OF ANY CONFLICTS OR DISCREPANCIES PRIOR TO CONSTRUCTION.
2. DO NOT SCALE DRAWINGS.
3. DIMENSIONS MARKED "CLR" ARE FROM FINISH SURFACE TO FINISH SURFACE.
4. SEE STRUCTURAL DRAWINGS FOR CONCRETE WALL THICKNESSES.
5. REFER TO SHEET A-101 TO A-103 FOR AIR BARRIER PLANS.

[illegible]

DESIGNED BY: WOOD	ISSUE DATE:
DRAWN BY: IROLOLO J MANUIA	SOLICITATION NO.:
CHECKED BY: MANUIA	CONTRACT NO.:
SUBMITTED BY:	W972HW-17-D-0003
SIZE:	

APO AP 96343-5010
FY20 MCA PN77833 VEHICLE MAINTENANCE SHOP

JMS - WALL SECTION (CLIN 0001)


SHEET ID

A-A311

INTERMEDIATE DESIGN

Plot Date: 12/17/2025 5:19:50 AM

Autodesk Docs://SSFM JED IDC VEHICLE MAINTENANCE SHOP/511758_TEMF_ARCH_ARCH_v2022.rvt

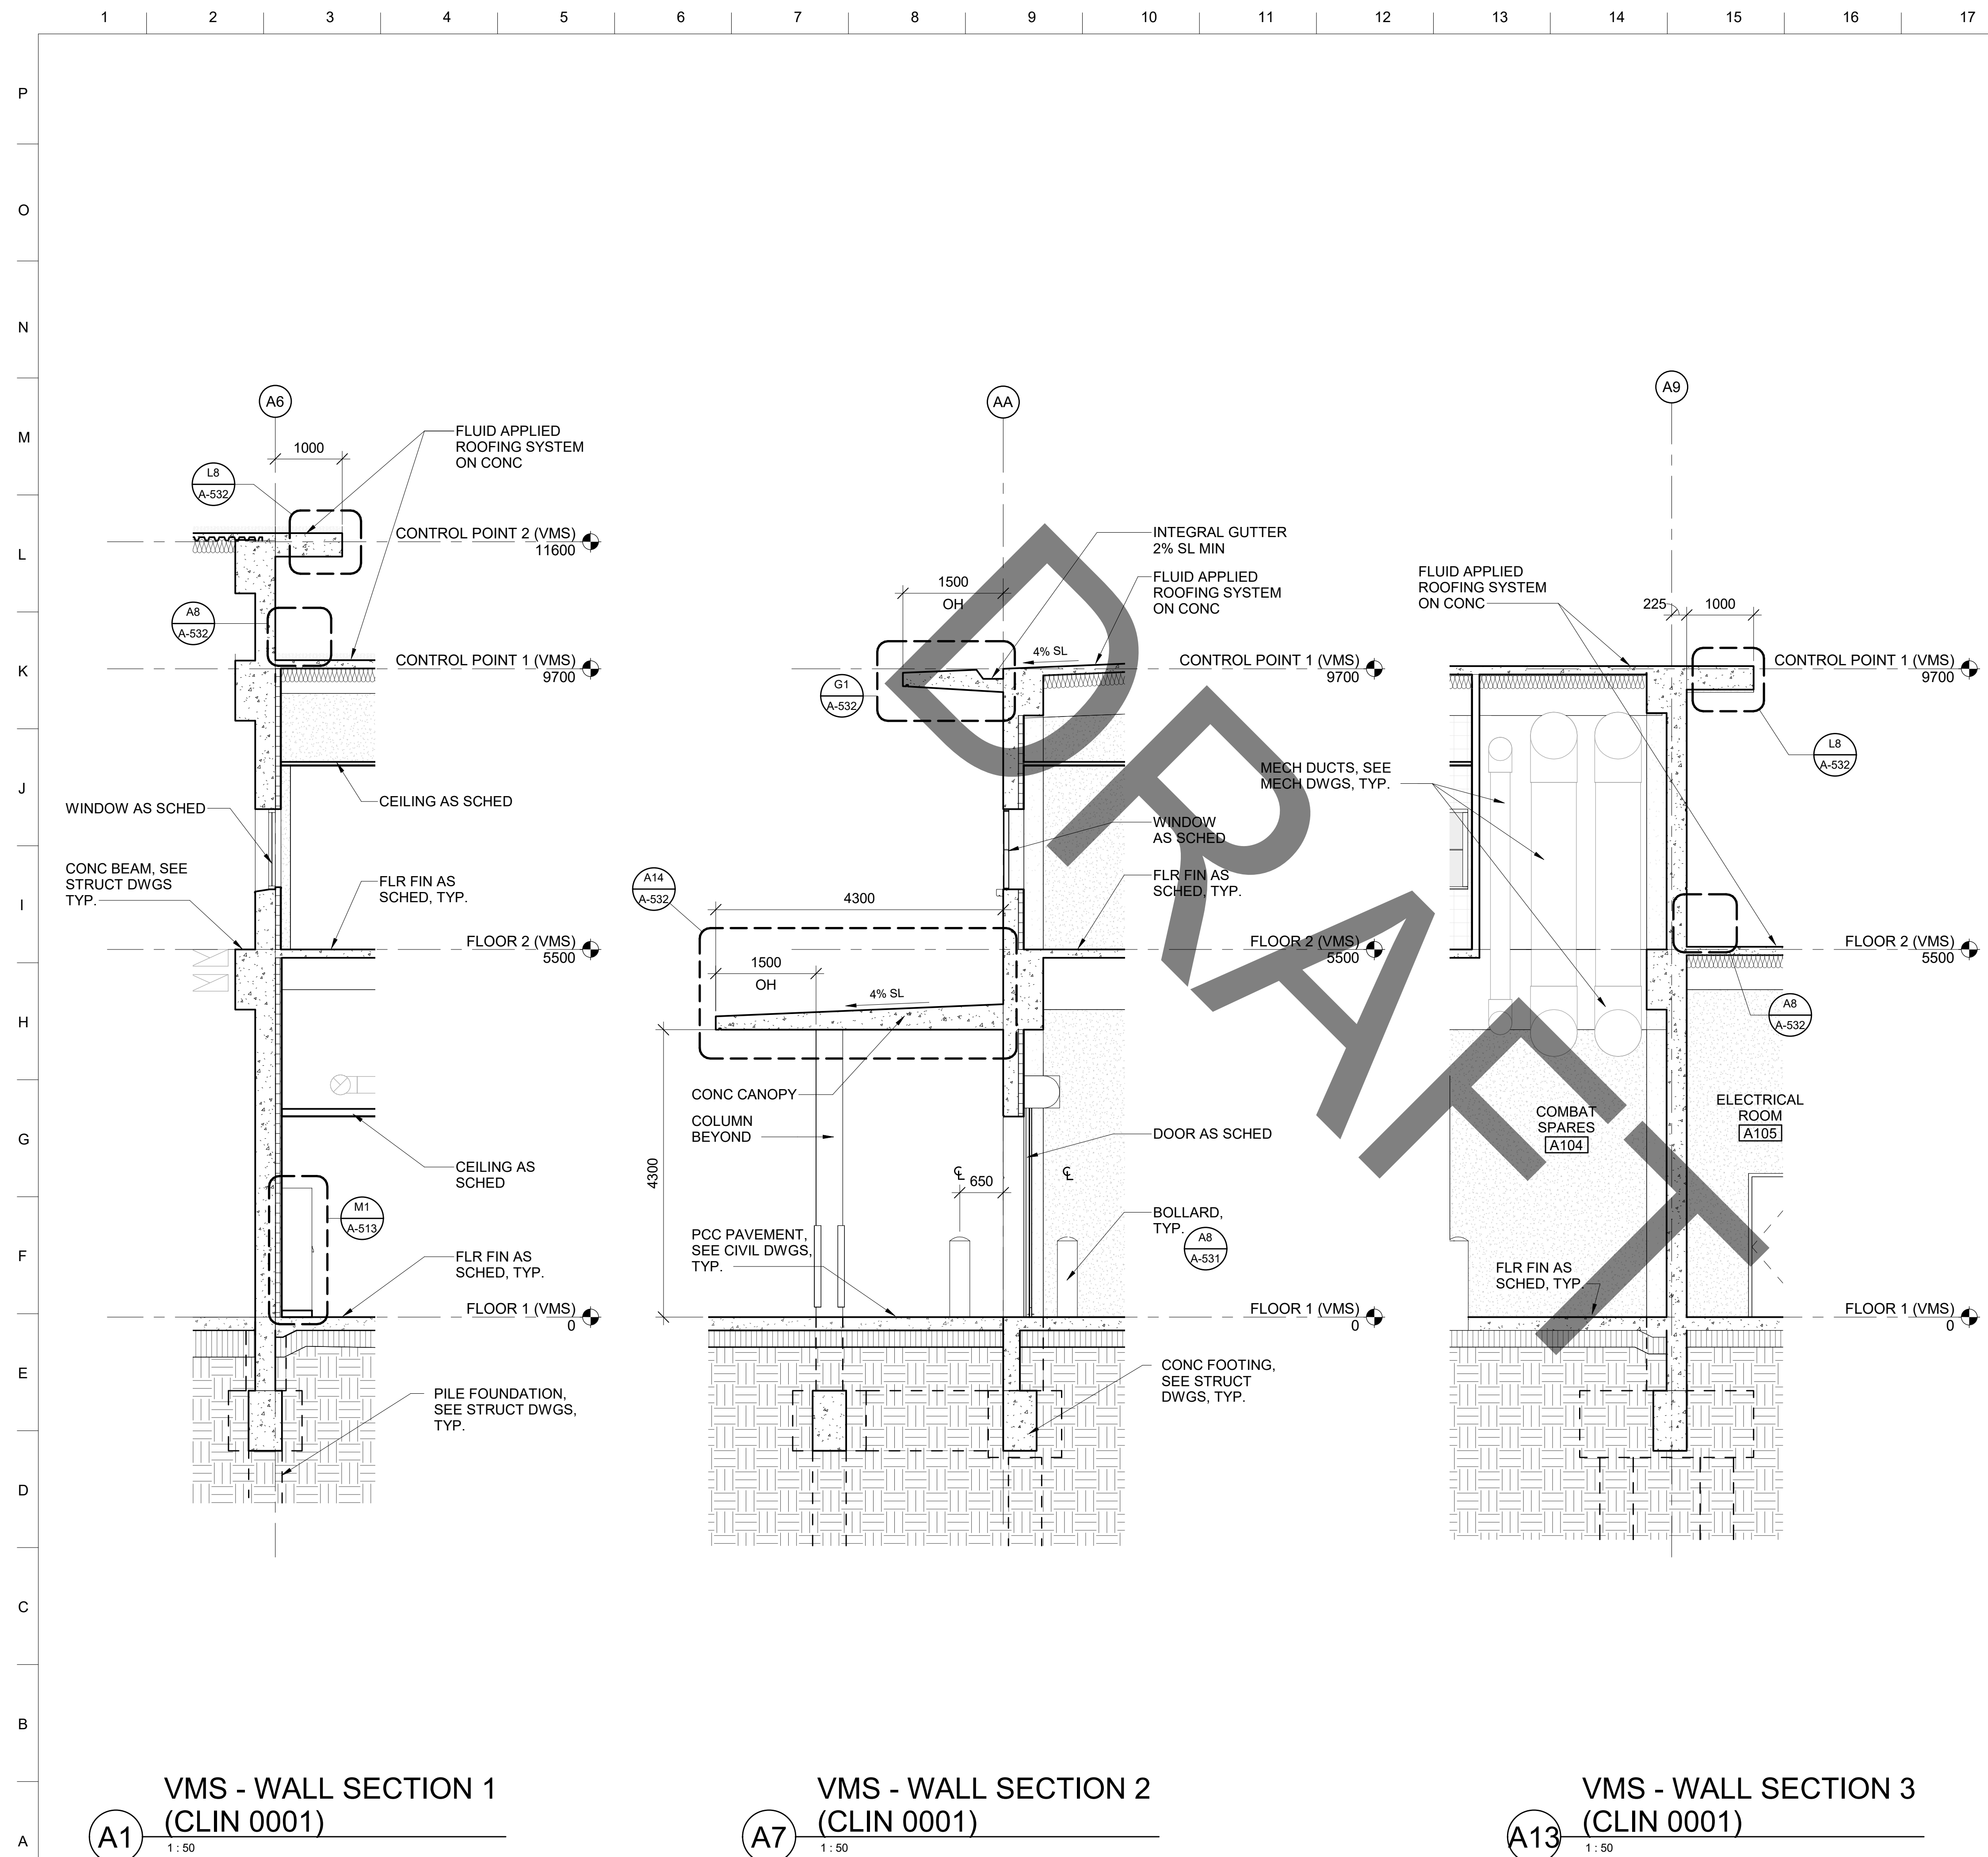

GENERAL NOTES

1. CONTRACTOR OR RESPONSIBLE PARTY TO FIELD VERIFY AND CONFIRM ALL DIMENSIONS AND LAYOUT INFORMATION. NOTIFY DESIGNER OF ANY CONFLICTS OR DISCREPANCIES PRIOR TO CONSTRUCTION.
2. DO NOT SCALE DRAWINGS.
3. DIMENSIONS MARKED "CLR" ARE FROM FINISH SURFACE TO FINISH SURFACE.
4. SEE STRUCTURAL DRAWINGS FOR CONCRETE WALL THICKNESSES.
5. REFER TO SHEET A-101 TO A-103 FOR AIR BARRIER PLANS.



**US Army Corps
of Engineers ®**

[illegible]

US ARMY CORPS OF ENGINEERS JAPAN ENGINEER DISTRICT OKINAWA AREA OFFICE APO AP 96376-5132	DESIGNED BY:	ISSUE DATE:
	DRAWN BY: CHECKED BY: Checker	SOLICITATION NO.: CONTRACT NO.: W912HJV-17-D-0003
DESIGN PARTNERS, INCORPORATED 1580 MAKALOA STREET, SUITE 1100 HONOLULU, HAWAII 96814	SUBMITTED BY:	
	SIZE: ANSI D	

APO AP 96343-5010
FY20 MCA PN77833 VEHICLE MAINTENANCE SHOP

VMS - WALL SECTION (CLIN 0001)

SHEET ID

A-A312

CLIN 0001

GRAPHIC SCALE




ALL DIMENSIONS AND/OR DIMENSIONS SHOWN IN
CALLOUT/ NOTES ARE IN MILLIMETERS UNLESS
OTHERWISE NOTED.

Autodesk Docs://SSFM JED IDC VEHICLE MAINTENANCE SHOP/511758 TEMF ARCH V2022.rvt

File Path:

Plot Date: 12/17/2025 5:10:53 AM

INTERMEDIATE DESIGN

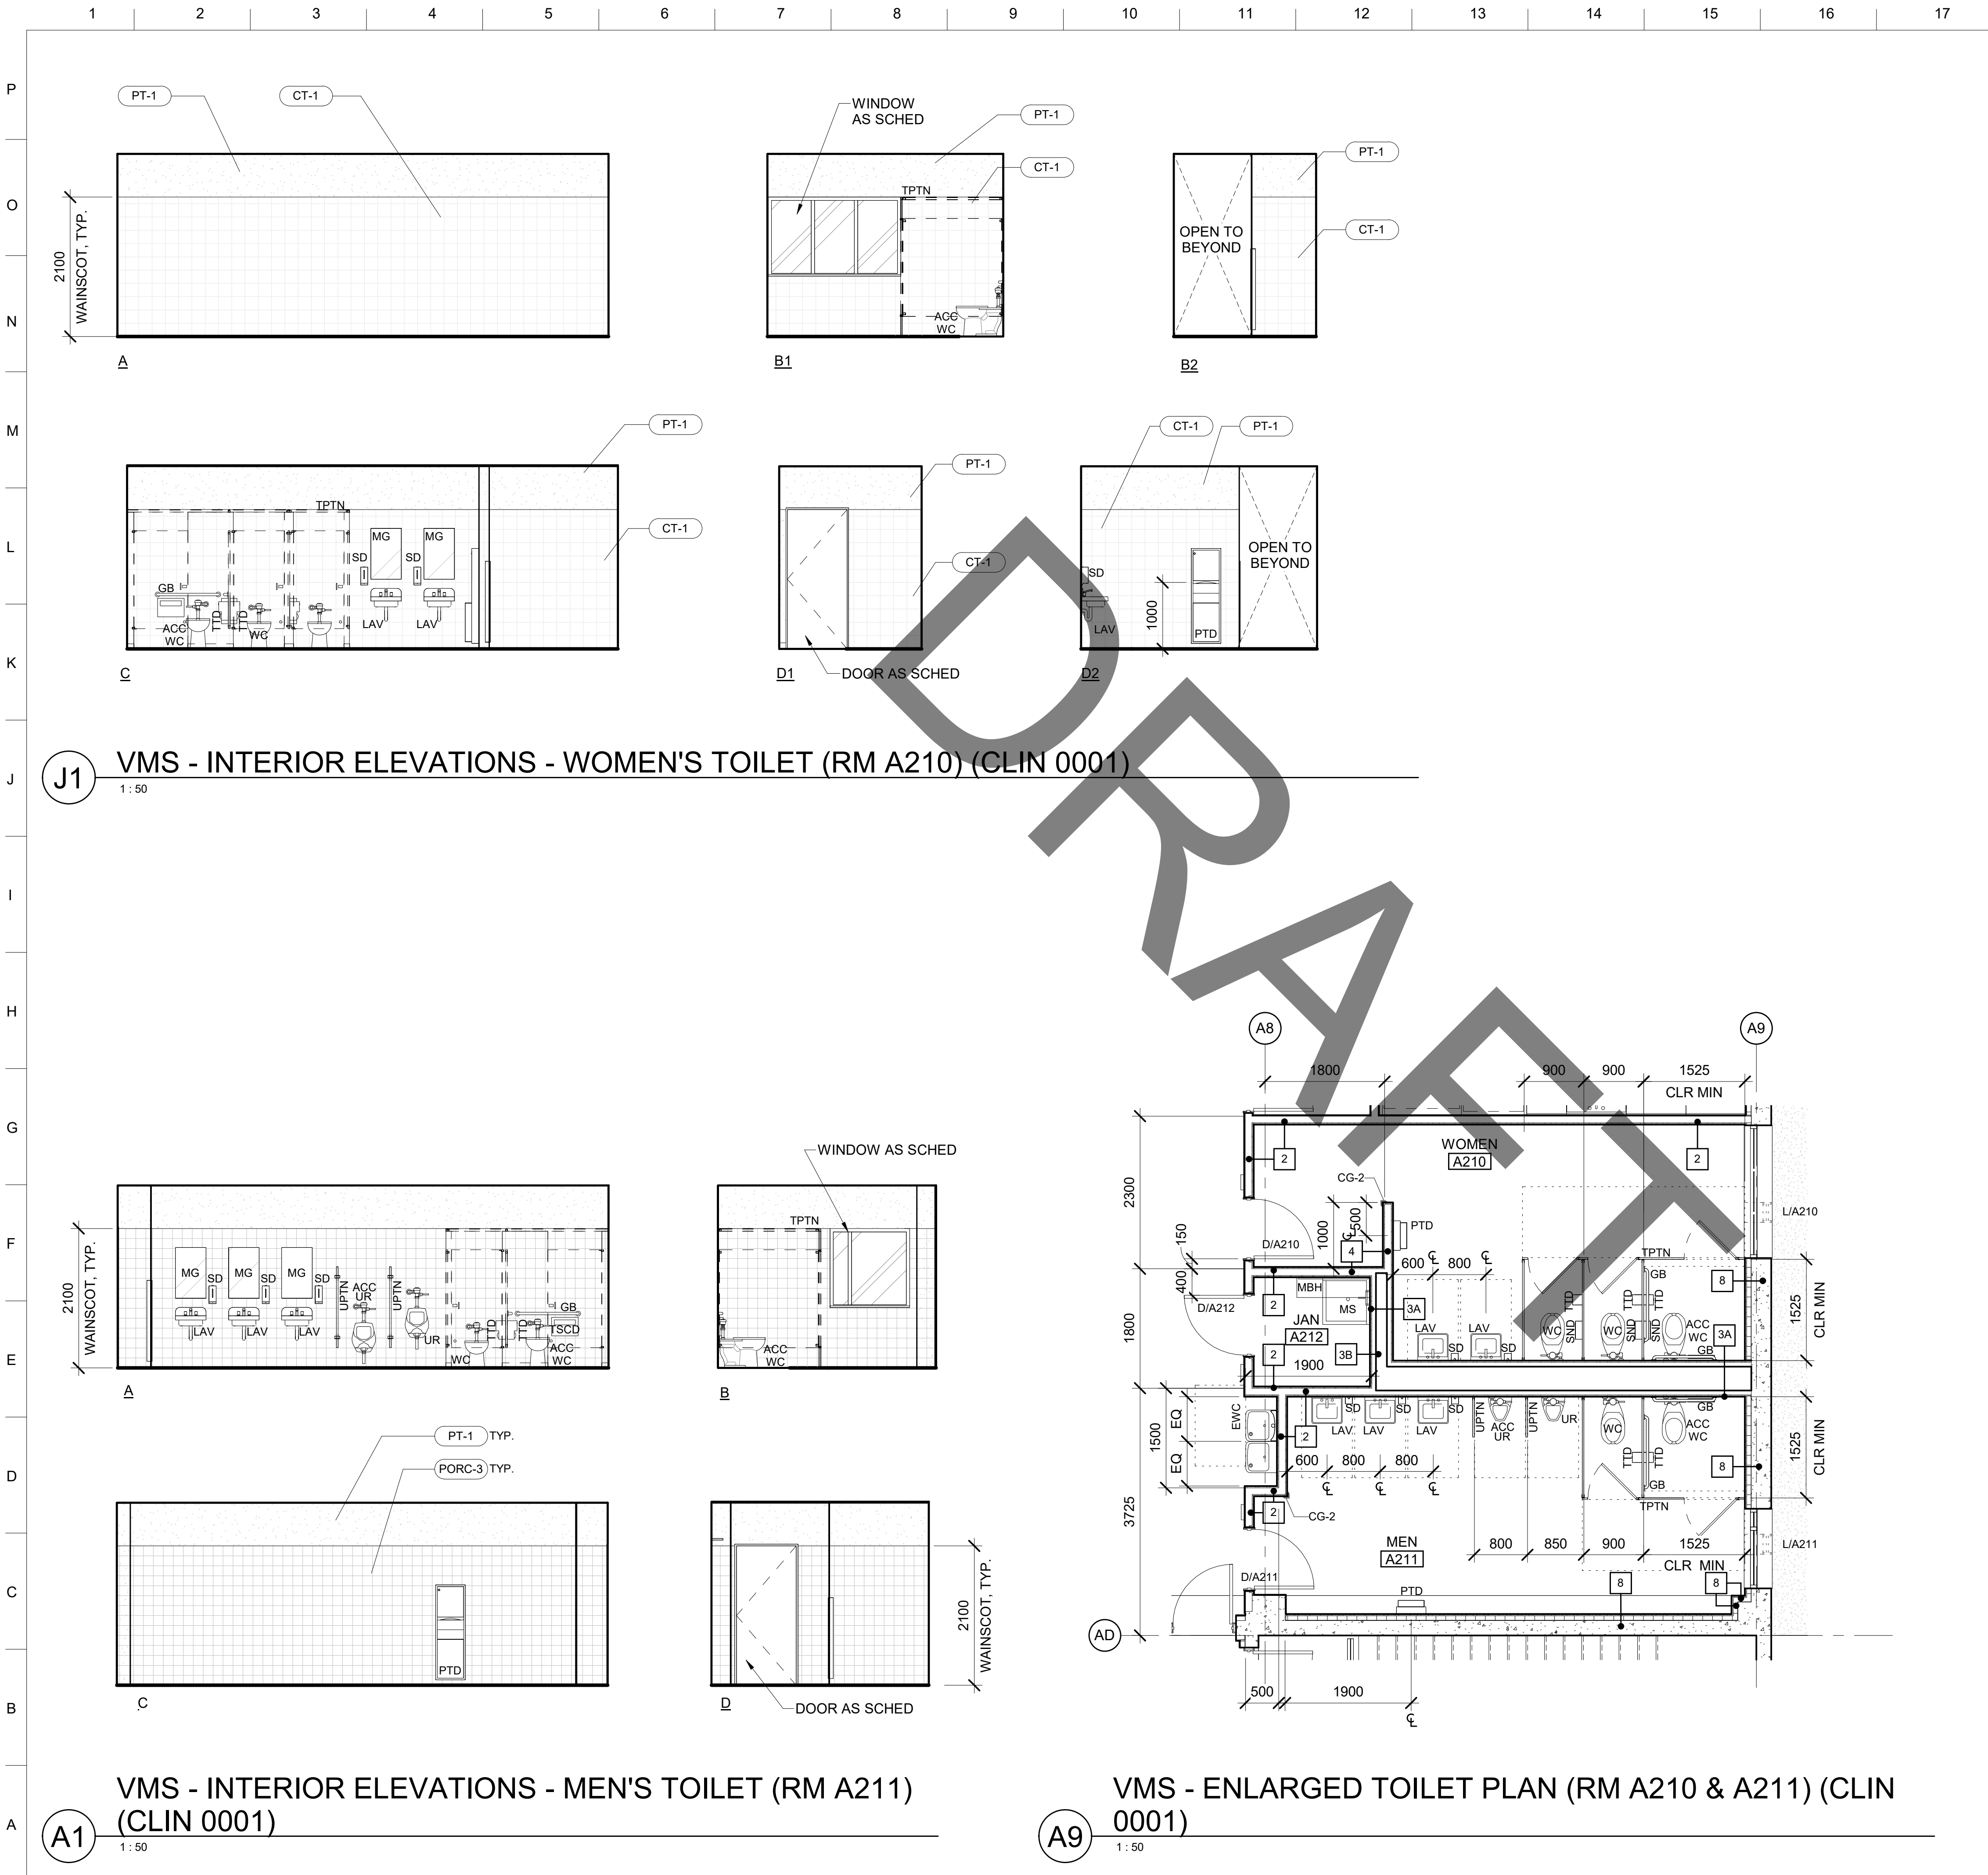

GENERAL NOTES

- DIMENSIONS MARKED "CLR" ARE FROM FINISH SURFACE TO FINISH SURFACE.
- FURNITURE AND EQUIPMENT ARE SHOWN IN DASHED FOR REFERENCE ONLY.
- REFER TO SHEET A-601 AND A-602 FOR DOOR SCHEDULES.
- REFER TO SHEET A-611 FOR WINDOW AND LOUVER SCHEDULES.
- REFER TO SHEET A-621 FOR MATERIAL FINISH SCHEDULES.
- REFER TO SHEET A-622 FOR ROOM FINISH SCHEDULES.

FIXTURE LEGEND - VMS

MARK	DESCRIPTION
ACC UR	ACCESSIBLE URINAL
EWC	ELECTRIC WATER COOLER
GB	GRAB BAR
LAV	LAVATORY
MBH	MOP AND BROOM WITH SHELF
MG	MIRROR, GLASS
MS	MOP SINK
PTD	PAPER TOWEL DISPENSER & TRASH RECEPTACLE
SD	SOAP DISPENSER, WALL MOUNTED
SND	SANITARY NAPKIN DISPOSAL
TPTN	TOILET PARTITION
TSCD	TOILET SEAT CIVER DISPENSER
TTD	TOILET TISSUE DISPENSER
UPTN	URINAL PARTITION
UR	URINAL
WC	WATER CLOSET
ACC WC	ACCESSIBLE WATER CLOSET

CLIN 0001

GRAPHIC SCALE

INT ELEV KEY

SCALE: 1 : 50

ALL DIMENSIONS AND/OR DIMENSIONS SHOWN IN CALLOUT/NOTES ARE IN MILLIMETERS UNLESS OTHERWISE NOTED.

010002000

US Army Corps of Engineers®

DESIGNED BY: KELLINGWOOD
DRAWN BY: IROLLO, J. MANUJA
CHECKED BY: W72AV-17-D-0003
SUBMITTED BY: SIZE: ANS/D

ISSUE DATE: SOLICITATION NO.: CONTRACT NO.: W72AV-17-D-0003

US ARMY CORPS OF ENGINEERS
JAPAN ENGINEER DISTRICT
OKINAWA AREA OFFICE
APO AP 96376-5132

DESIGN PARTNERS INCORPORATED
1580 MAKALOA STREET, SUITE 1100
HONOLULU, HAWAII 96814

APO AP 96343-5010
FY20 MCA PN77833 VEHICLE MAINTENANCE SHOP


VMS - ENLARGED FLOOR PLAN AND INTERIOR ELEVATIONS - MEN'S (RM A211) AND WOMEN'S TOILET (RM A210) (CLIN 0001)

SHEET ID

A-A402

Plot Date: 12/17/2025 5:20:21 AM

File Path: Autocad Docs/SPN/VED DC VEHICLE MAINTENANCE SHOP/511795_T/EMF_Arch_V02214

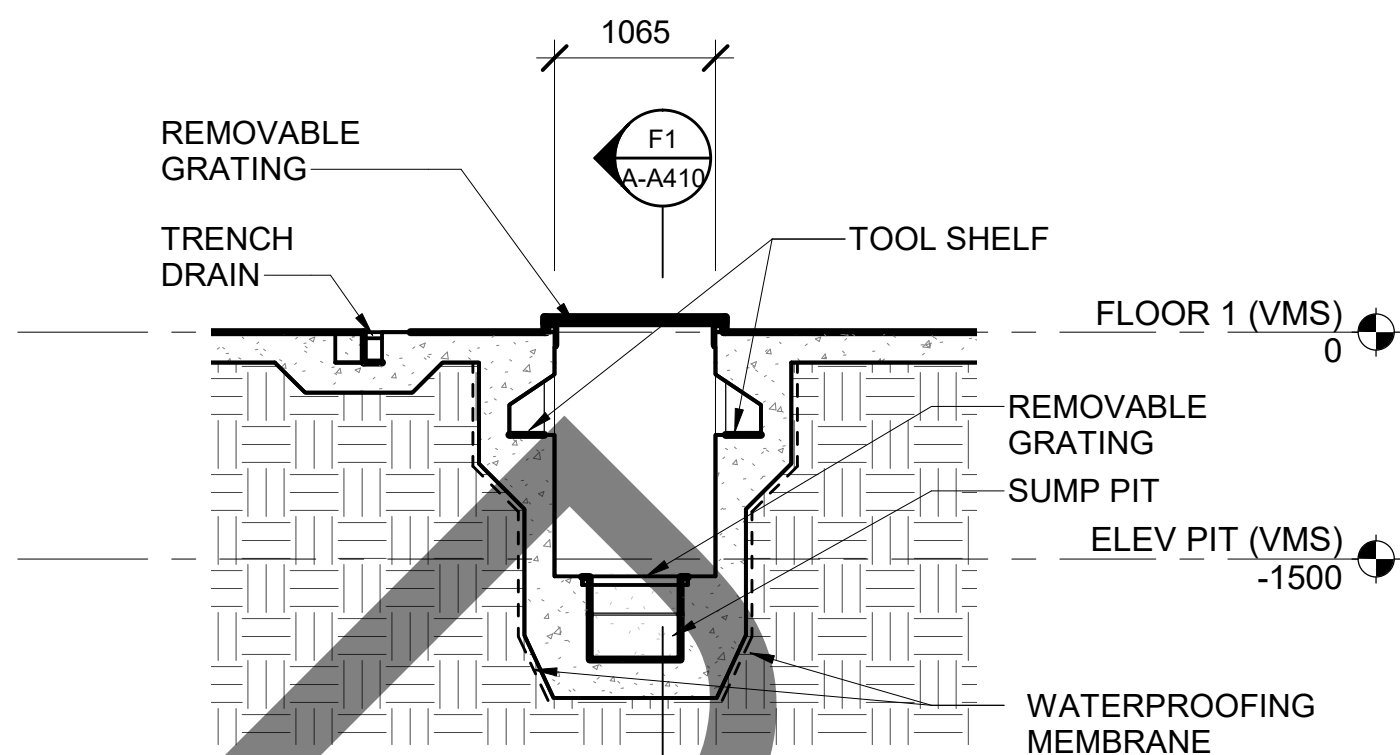

SECTION - TRANSVERSE - MAINTENANCE
PIT

[illegible]

1. DIMENSIONS MARKED "CLR" ARE FROM FINISH SURFACE TO FINISH SURFACE.
2. FURNITURE AND EQUIPMENT ARE SHOWN IN DASHED FOR REFERENCE ONLY.
3. REFER TO SHEET A-601 AND A-602 FOR DOOR SCHEDULES.
4. REFER TO SHEET A-611 FOR WINDOW AND LOUVER SCHEDULES.
5. REFER TO SHEET A-621 FOR MATERIAL FINISH SCHEDULES.
6. REFER TO SHEET A-622 FOR ROOM FINISH SCHEDULES.

DESIGNED BY: K.ELLINGWOOD	DESIGNED BY: K.ELLINGWOOD	ISSUE DATE:	CONTRACT NO.: W912HV-17-D-0003	CONTRACT NO.: W912HV-17-D-0003	SIGNED:	DATE:
DRAWN BY: J. MANUUA	DRAWN BY: J. MANUUA	CHECKED BY: D. MOATES	CHECKED BY: D. MOATES	SIGNED:	DATE:	DATE:
US ARMY CORPS OF ENGINEERS JAPAN ENGINEER DISTRICT OKINAWA AREA OFFICE APO AF 96376-5132						
DESIGN PARTNERS INCORPORATED 1550 MANALOA STREET, SUITE 1100 HONOLULU, HAWAII 96814						

WMS - ENLARGED PLAN AND SECTIONS - MAINTENANCE PIT (CLIN 0001)


SHEET ID

A-A410


CLIN 0001

GRAPHIC SCALE

SCALE: 1 : 50

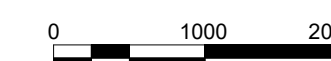

ALL DIMENSIONS AND/OR DIMENSIONS SHOWN IN
CALLOUT/ NOTES ARE IN MILLIMETERS UNLESS
OTHERWISE NOTED.

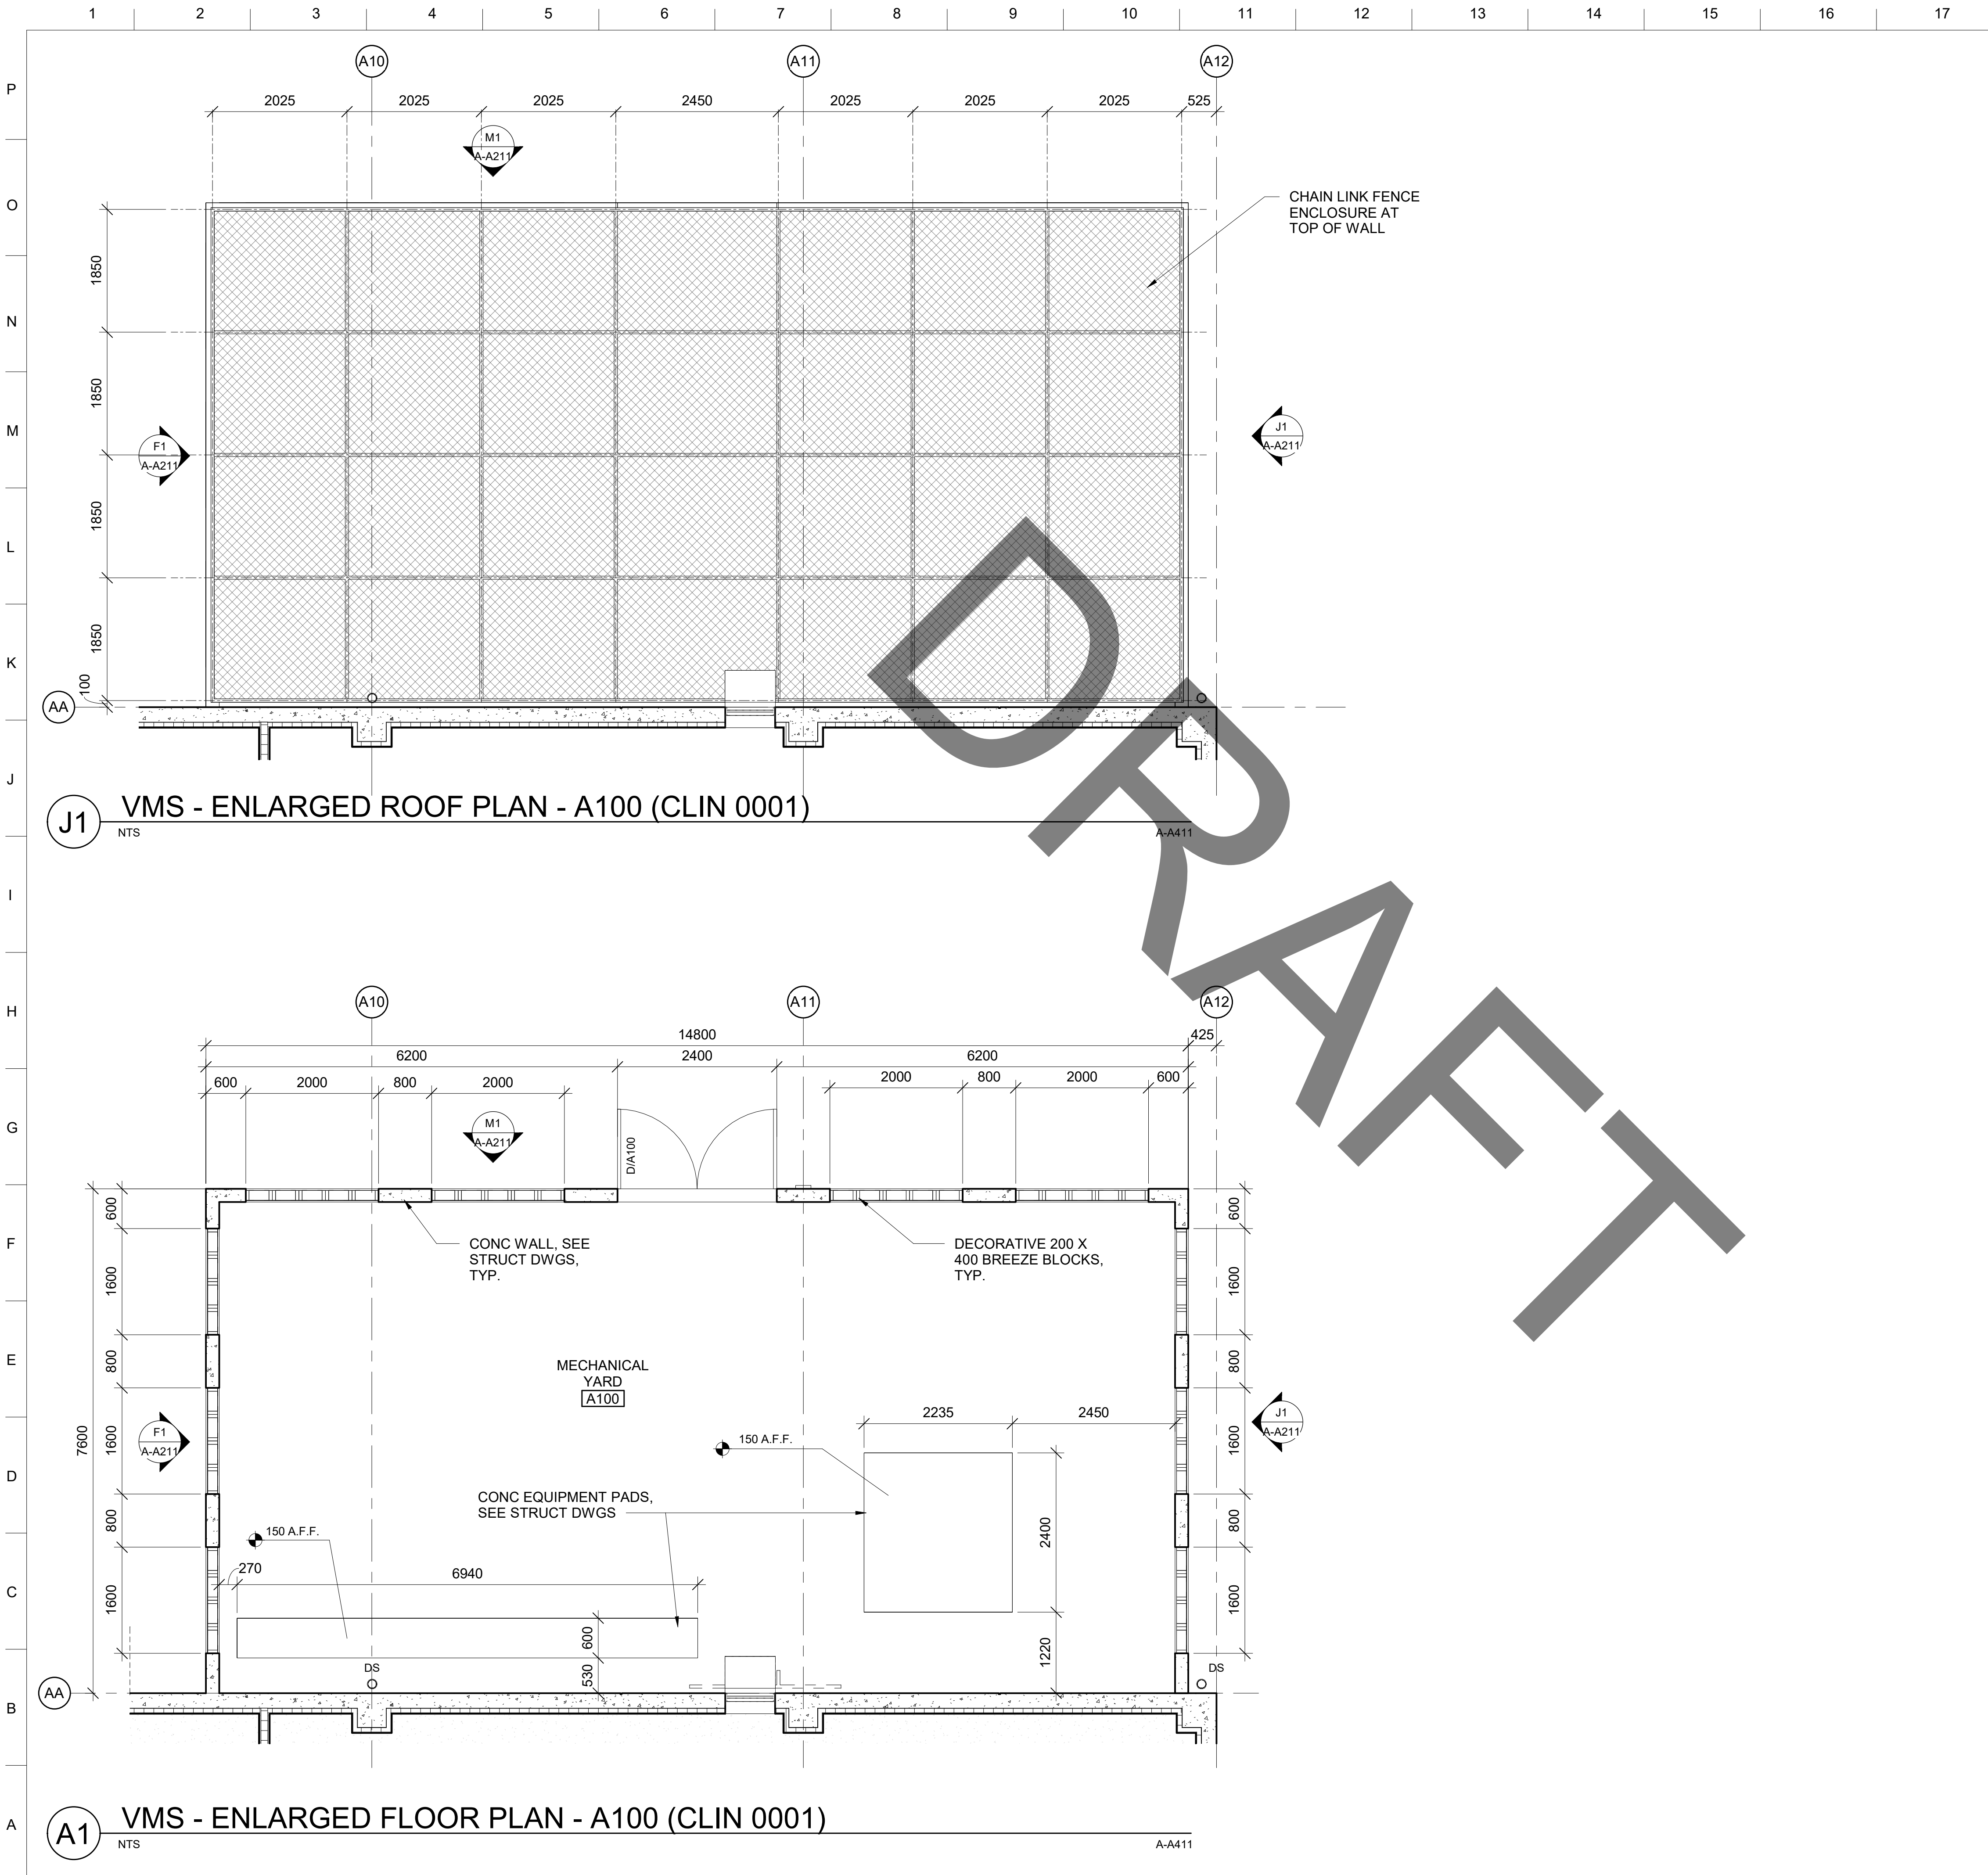

GENERAL NOTES

1. DIMENSIONS MARKED "CLR" ARE FROM FINISH SURFACE TO FINISH SURFACE.
2. FURNITURE AND EQUIPMENT ARE SHOWN IN DASHED FOR REFERENCE ONLY.
3. REFER TO SHEET A-601 AND A-602 FOR DOOR SCHEDULES.
4. REFER TO SHEET A-611 FOR WINDOW AND LOUVER SCHEDULES.
5. REFER TO SHEET A-621 FOR MATERIAL FINISH SCHEDULES.
6. REFER TO SHEET A-622 FOR ROOM FINISH SCHEDULES.



US Army Corps
of Engineers ®

MARK	DESCRIPTION	DATE

DESIGNED BY: K. LELAND	ISSUE DATE:
DRAWN BY: J. MANUJA	SOLICITATION NO.:
CHECKED BY:	CONTRACT NO.:
SUBMITTED BY:	W72WY-17-D-0003
SIZE: ANSI D	

US ARMY CORPS OF ENGINEERS JAPAN ENGINEER DISTRICT OKINAWA AREA OFFICE APO AP 96376-5132	DESIGN PARTNERS INCORPORATED 1580 MAKALOA STREET, SUITE 1100 HONOLULU, HAWAII 96814
---	---

Autodesk Docs/ISSUED DOC VEHICLE MAINTENANCE SHOP11795_TEMF_ARCH_V02214

File Path:


Plot Date: 12/17/2025 5:20:38 AM

INTERMEDIATE DESIGN

CLIN 0001

GRAPHIC SCALE

PLAN
NORTH

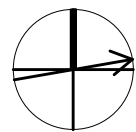

SCALE: 1 : 50




ALL DIMENSIONS AND/OR DIMENSIONS SHOWN IN
CALLOUT/ NOTES ARE IN MILLIMETERS UNLESS
OTHERWISE NOTED.

APO AP 96343-5010
FY20 MCA PN7833 VEHICLE MAINTENANCE SHOP
VMS - ENLARGED PLAN AND ELEVATIONS - MECHANICAL YARD
(CLIN 0001)


SHEET ID

A-A411

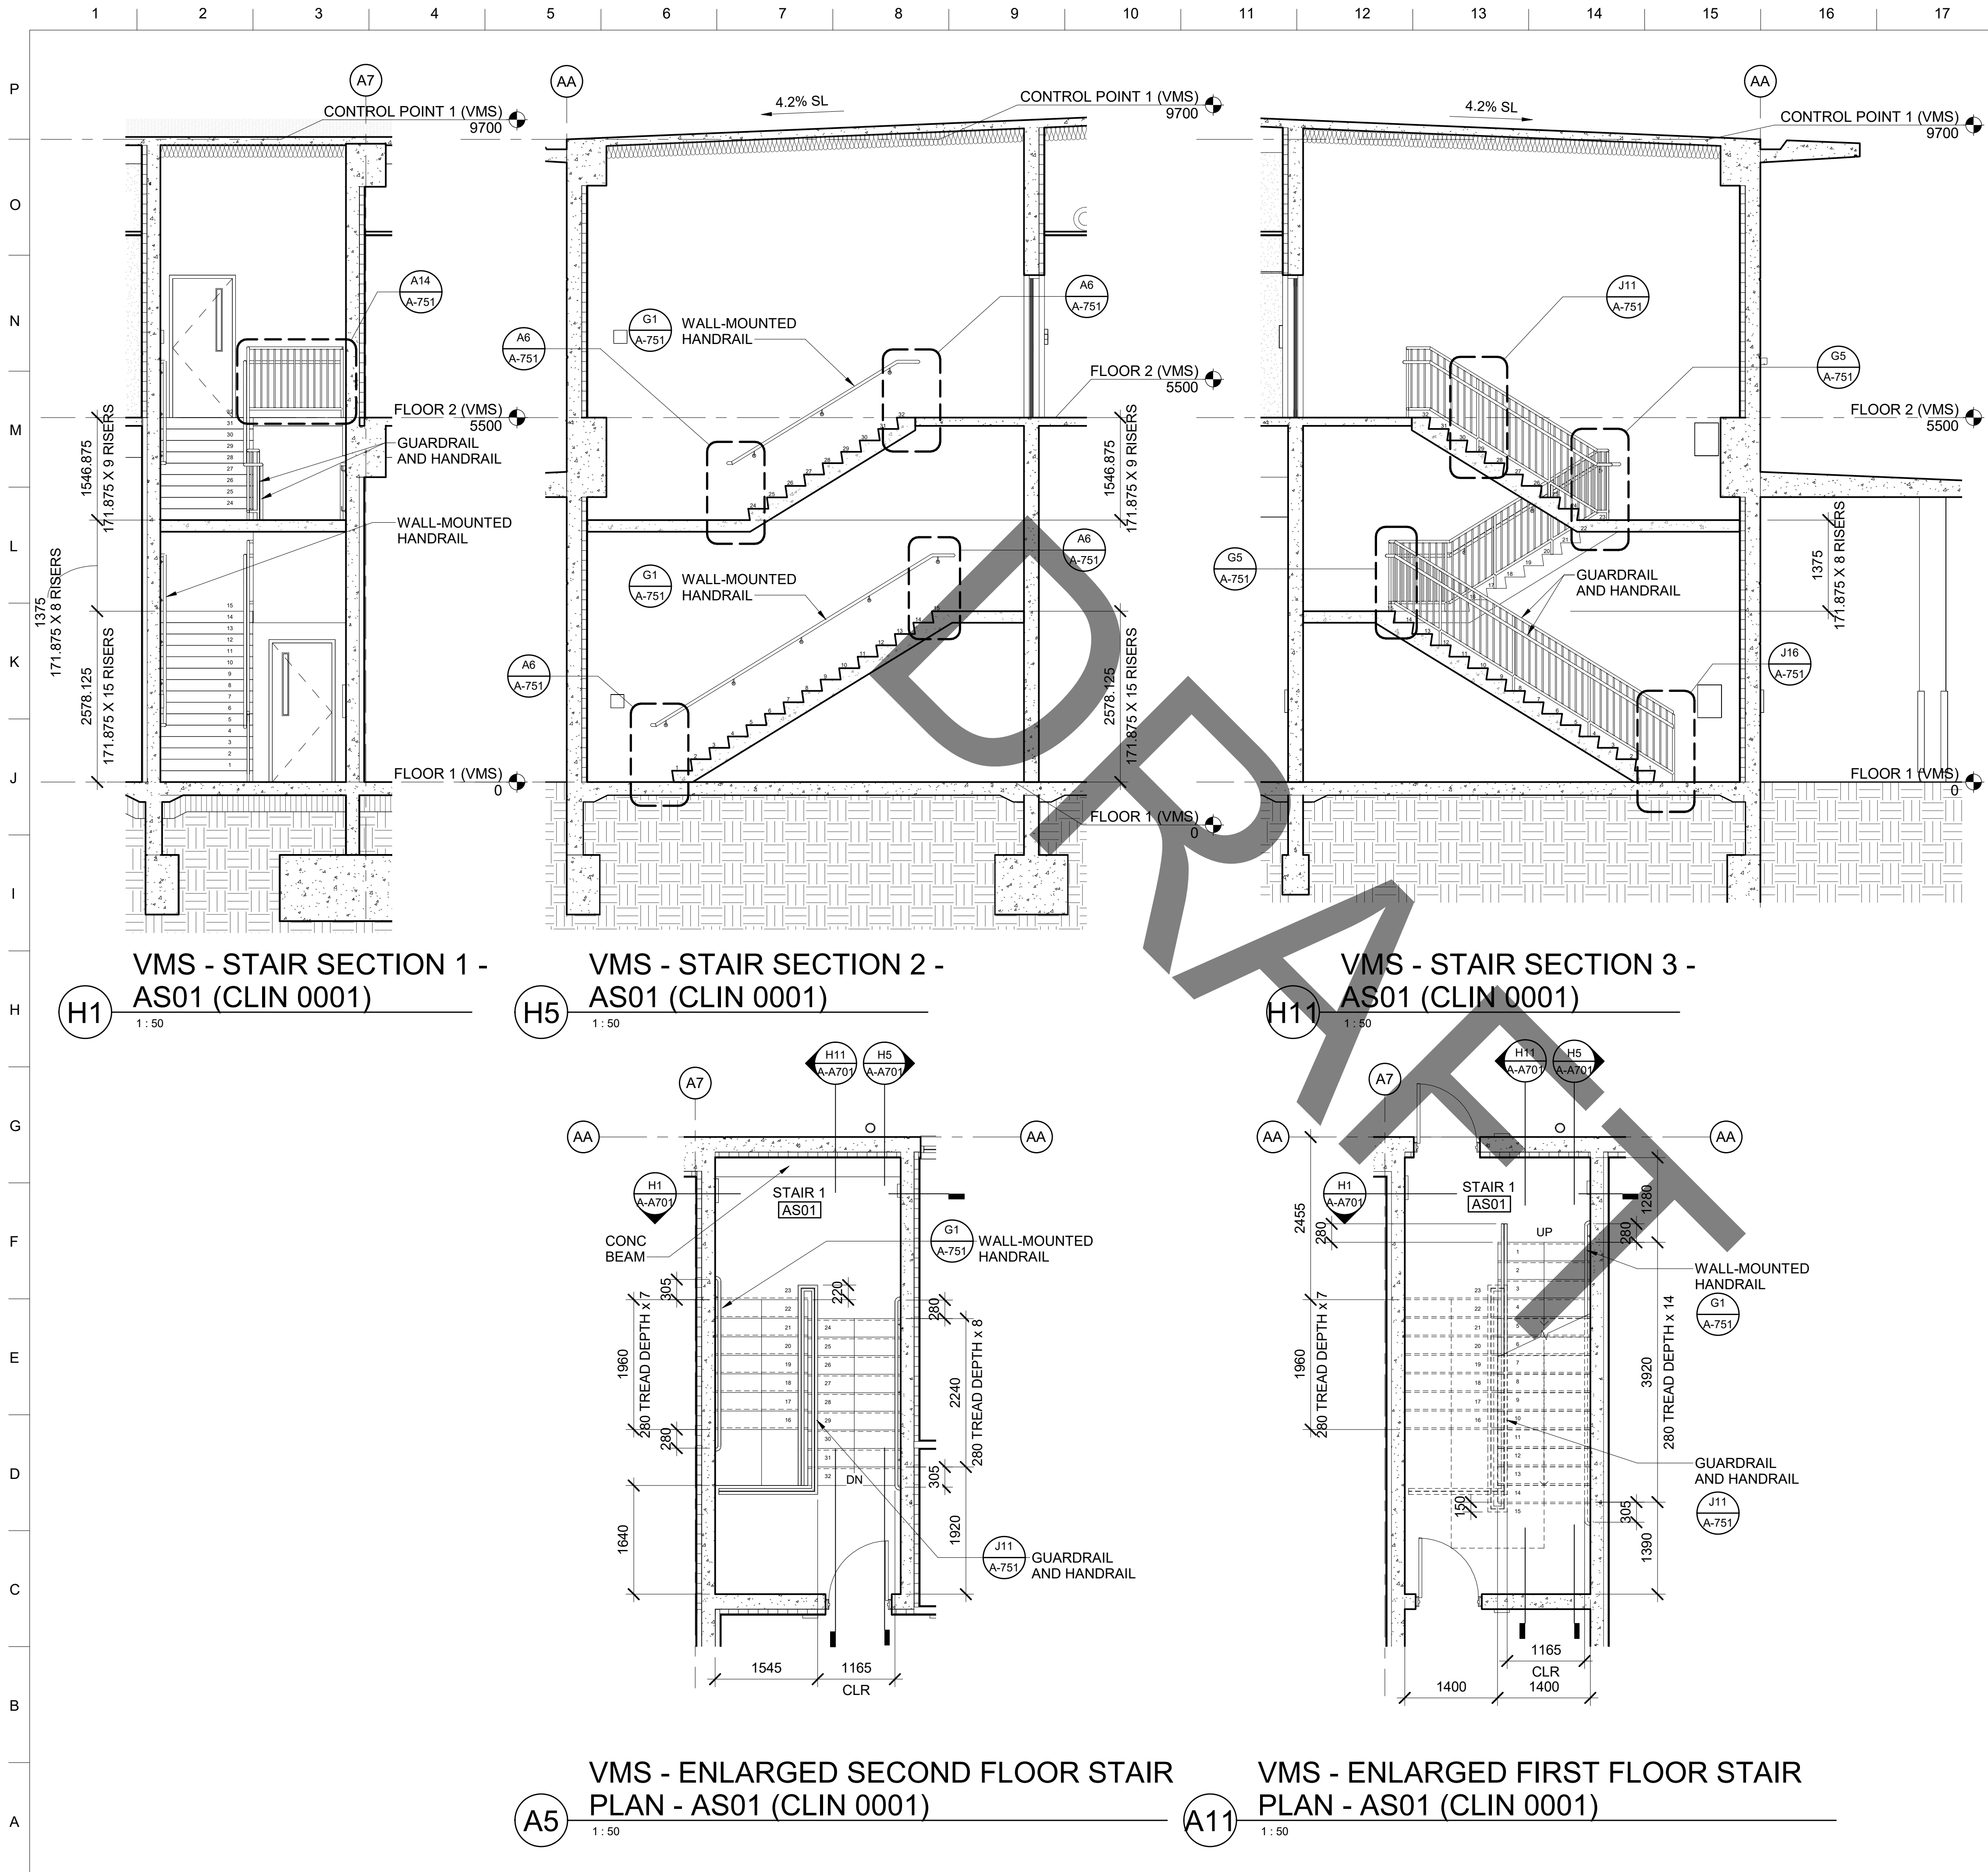

GENERAL NOTES

1. DIMENSIONS MARKED "CLR" ARE FROM FINISH SURFACE TO FINISH SURFACE.
2. FURNITURE AND EQUIPMENT ARE SHOWN IN DASHED FOR REFERENCE ONLY.
3. REFER TO SHEET A-601 AND A-602 FOR DOOR SCHEDULES.
4. REFER TO SHEET A-611 FOR WINDOW AND LOUVER SCHEDULES.
5. REFER TO SHEET A-621 FOR MATERIAL FINISH SCHEDULES.
6. REFER TO SHEET A-622 FOR ROOM FINISH SCHEDULES.

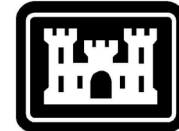

US Army Corps
of Engineers ®

MARK	DESCRIPTION	DATE

DESIGNED BY: K. KELINGWOOD	ISSUE DATE:
DRAWN BY: I. ROLLO, J. MANUJA	SOLICITATION NO.:
CHECKED BY: W. J. RYAN, J. D. GREGG	CONTRACT NO.:
SUBMITTED BY:	
SIZE: ANSI D	

US ARMY CORPS OF ENGINEERS
JAPAN ENGINEER DISTRICT
OKINAWA AREA OFFICE
APO AP 96376-5132

DESIGN PARTNERS INCORPORATED
1580 MAKALOA STREET, SUITE 1100
HONOLULU, HAWAII 96814

Autodesk Docs/ISSUED DOC: VEHICLE MAINTENANCE SHOP11709_TEMPL_A-601_0002.rvt

File Path:

Plot Date: 12/17/2025 5:20:40 AM

INTERMEDIATE DESIGN

GRAPHIC SCALE

SCALE: 1 : 50




ALL DIMENSIONS AND/OR DIMENSIONS SHOWN IN
CALLOUT/ NOTES ARE IN MILLIMETERS UNLESS
OTHERWISE NOTED.

APO AP 96343-50110
FY20 MCA PN77833 VEHICLE MAINTENANCE SHOP

VMS - ENLARGED STAIR FLOOR PLAN AND SECTION - AS01 (CLIN 0001)

SHEET ID

A-A701

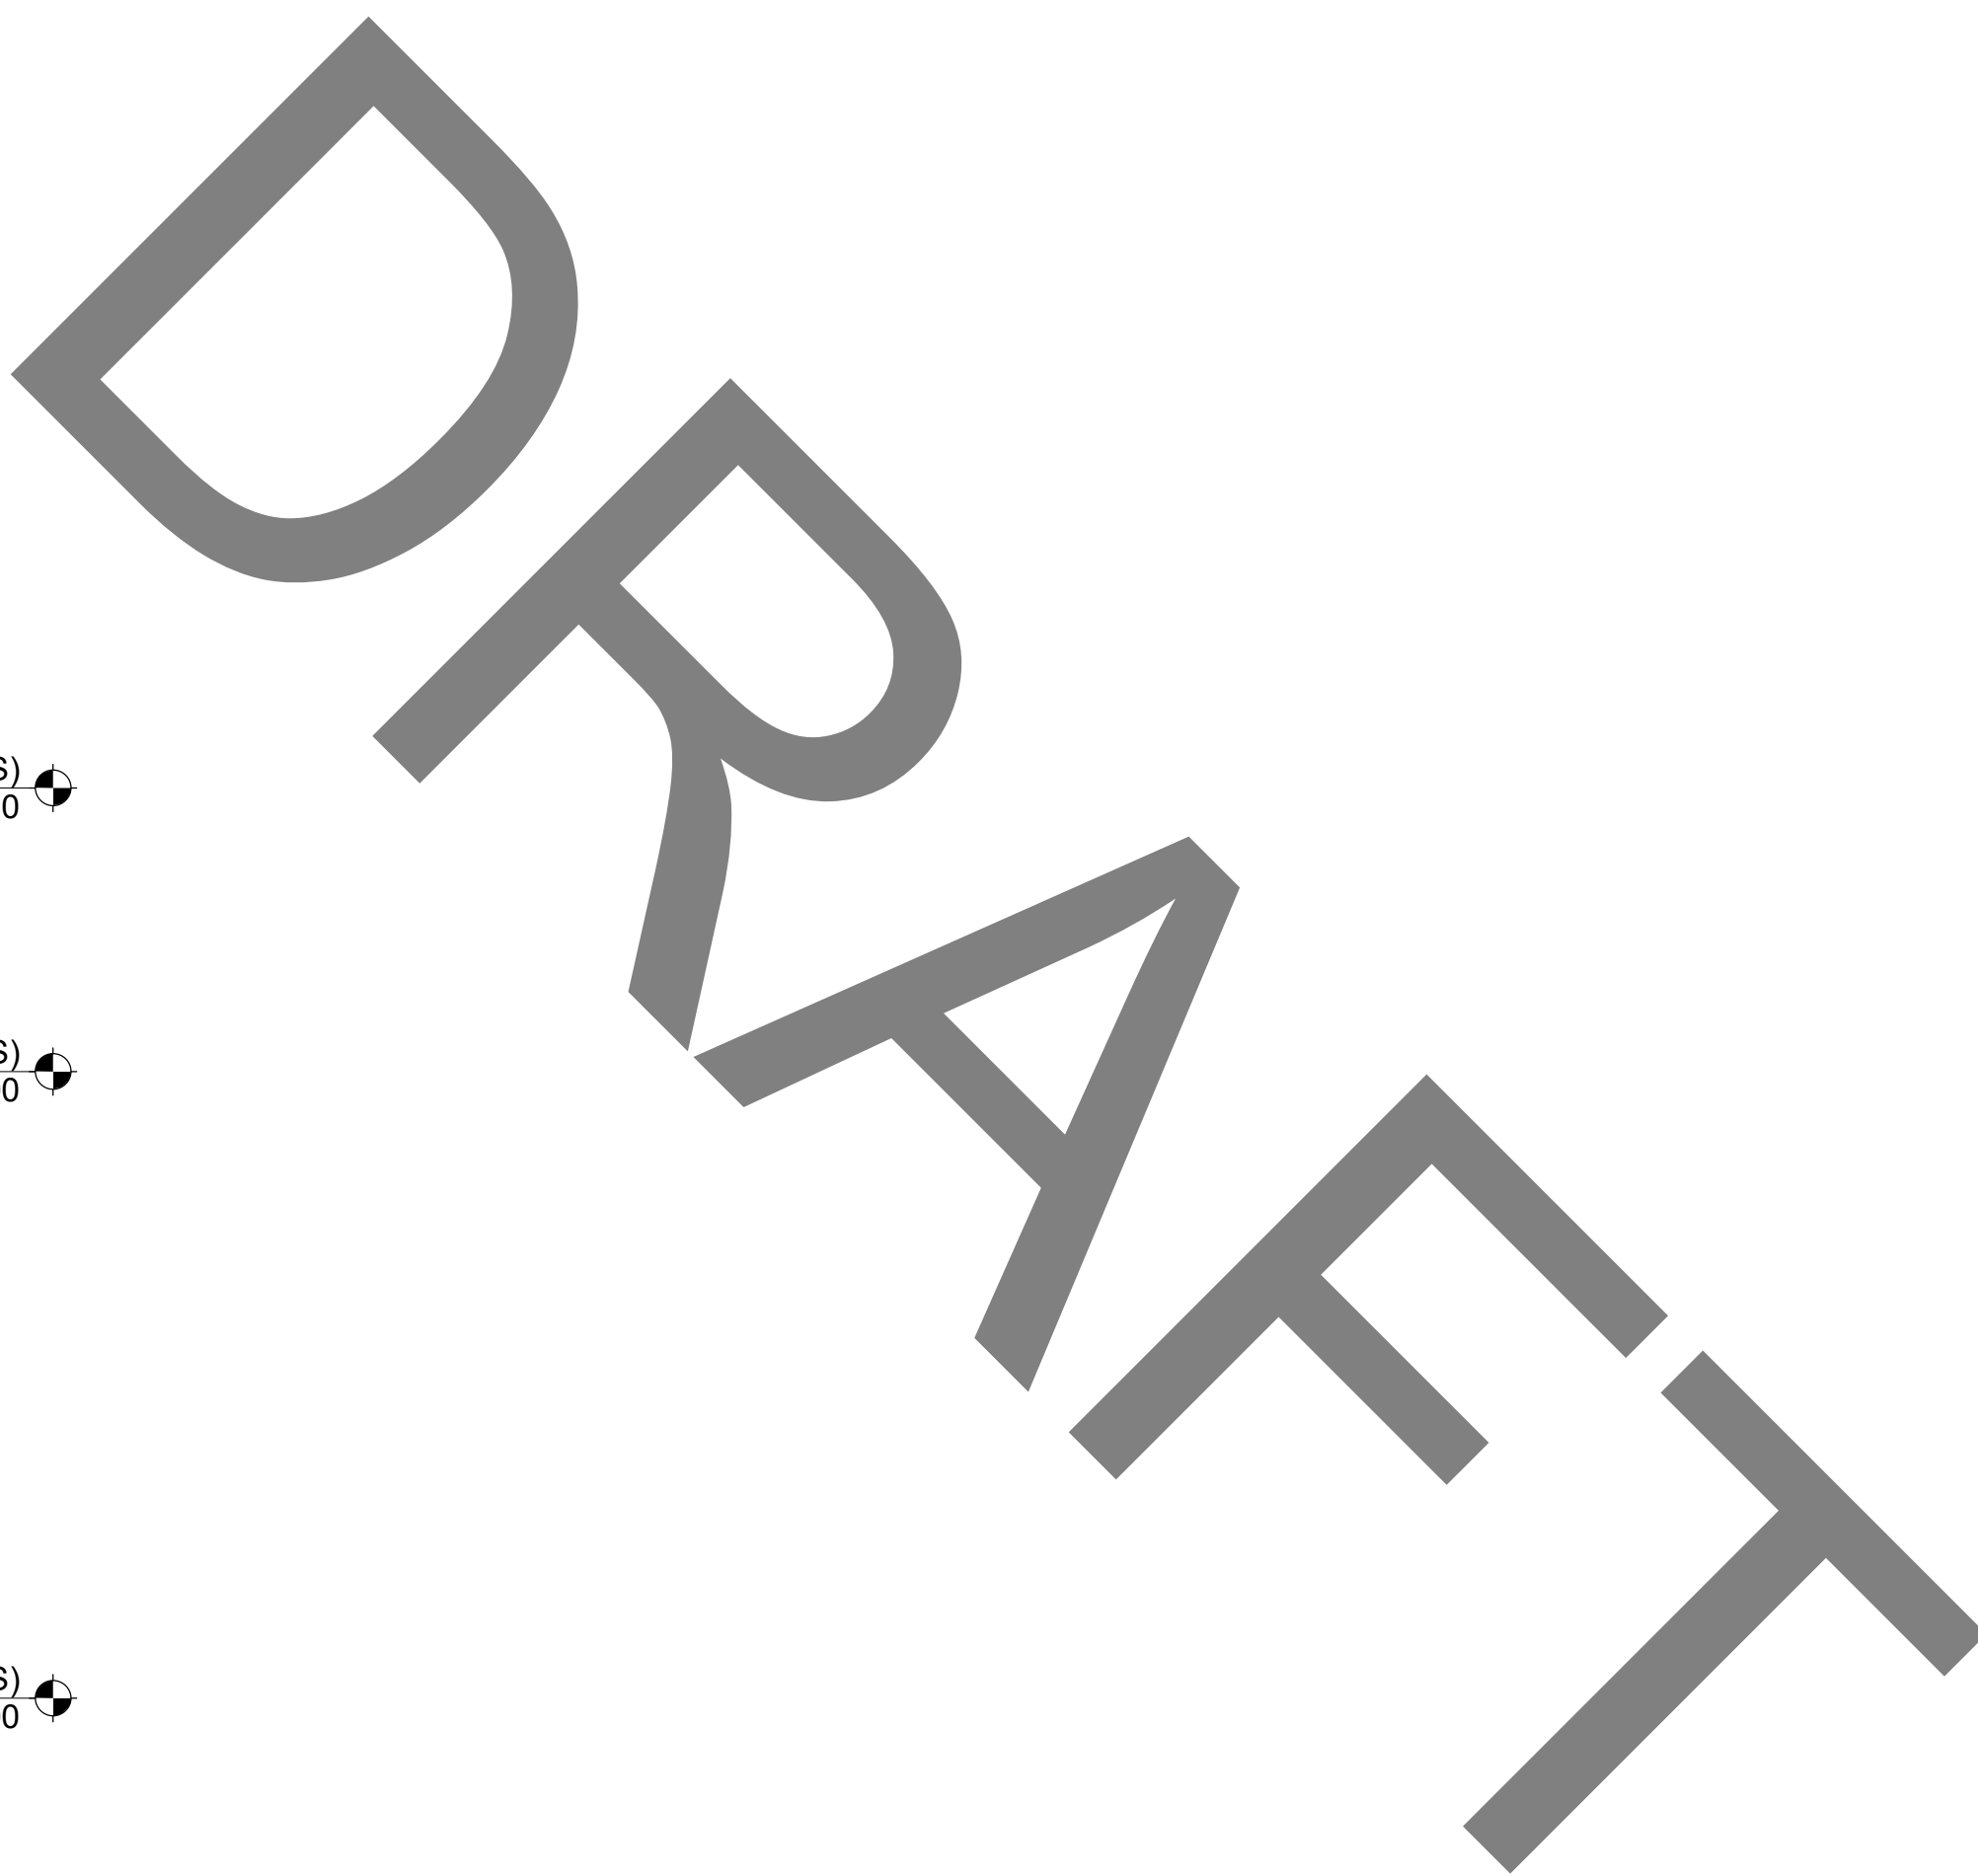

K1

Architectural section drawing showing a building with multiple levels and structural details. The drawing includes the following elements and dimensions:

- Roofing:** FLUID-APPLIED ROOFING SYSTEM ON CONC. TYP. with a 4.2% SL (slope).
- Integral Gutter:** INTEGRAL GUTTER 5% SL MIN.
- Control Points:**
 - CONTROL POINT 2 (VMS) 11600
 - CONTROL POINT 1 (VMS) 9700
- Structural Details:**
 - STEEL RAILINGS
 - STEEL LADDER
 - DOOR AS SCHED
 - 300 DIA BOLLARDS, TYP.
- Dimensions:**
 - 5000 (horizontal distance)
 - 1100 (vertical distance)
 - 1300 (vertical distance)
 - 2000 (horizontal distance)
 - 1500 (horizontal distance)
 - 3500 (horizontal distance)
 - 3000 (vertical distance)
 - 1500 (horizontal distance)
 - 300 (vertical distance)
- Other Labels:**
 - A14 A-532
 - MACHINE SHOP/ WELDING AREA A101A
 - T.O.W. (VMS) 2100
 - FLOOR 2 (VMS) 5500
 - FLOOR 1 (VMS) 0
 - ELEV PIT (VMS) -1500

A1

ALL DIMENSIONS AND/OR DIMENSIONS SHOWN IN
CALLOUT/ NOTES ARE IN MILLIMETERS UNLESS
OTHERWISE NOTED.