



HIGH-HAZARD STORAGE

[illegible]

US ARMY CORPS OF ENGINEERS JAPAN ENGINEER DISTRICT ENGINEERING CENTER APO AP 96376-5132	DESIGNED BY: C. RYUNYON	ISSUE DATE:
DESIGN PARTNERS, INCORPORATED 1580 MAKALOA STREET, SUITE 1100 HONOLULU, HAWAII 96814	DRAWN BY: K. LEE	SOLICITATION NO.: CONTRACT NO.:
	CHECKED BY: B. JIMON	WB12HV-17-D-0003
	SUBMITTED BY:	
	DATE: ANS'D	

FY20 MCA PN77833 VEHICLE MAINTENANCE SHOP
KADENA AIR BASE, OKINAWA, JAPAN

OS - FIRE SPRINKLER PLAN (CLIN 0002)

SHEET ID

FXB101

INTERMEDIATE DESIGN

Plot Date:

12/16/2025 10:27:16 AM

File Path:

C:\Users\klee\Documents\511758_OS_FIRE_v2022_klee\WVXJU.rvt

PLAN
NORTH




GRAPHIC SCALE

SCALE: 1 : 100




ALL DIMENSIONS AND/OR DIMENSIONS SHOWN IN
CALLOUT/ NOTES ARE IN MILLIMETERS UNLESS
OTHERWISE NOTED.

FXB101

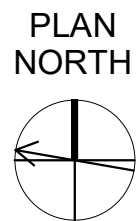

GRAPHIC SCALE

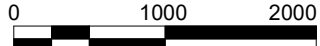

SCALE: 1 : 50

ALL DIMENSIONS AND/OR DIMENSIONS SHOWN IN
CALLOUT/ NOTES ARE IN MILLIMETERS UNLESS
OTHERWISE NOTED.



**US Army Corps
of Engineers ®**

[illegible]


US ARMY CORPS OF ENGINEERS JAPAN ENGINEER DISTRICT KINAWA AREA OFFICE APO AP 96376-5132	DESIGNED BY: C. RUYON	ISSUE DATE:
	DRAWN BY: K. LEWIS CHECKED BY: B. JIM ON	SOLICITATION NO.: CONTRACT NO.: W612HW-17-D-0003
DESIGN PARTNERS INCORPORATED 1580 MAKALOA STREET, SUITE 1100 HONOLULU, HAWAII 96814	SUBMITTED BY: SIZE: ANSI D	



FY20 MCA PN77833 VEHICLE MAINTENANCE SHOP
KADENA AIR BASE, OKINAWA, JAPAN

POL & HAZMAT STORAGE - FIRE SPRINKLER PLAN (CLIN 0002)

SHEET ID

FXC101

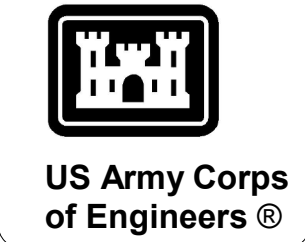

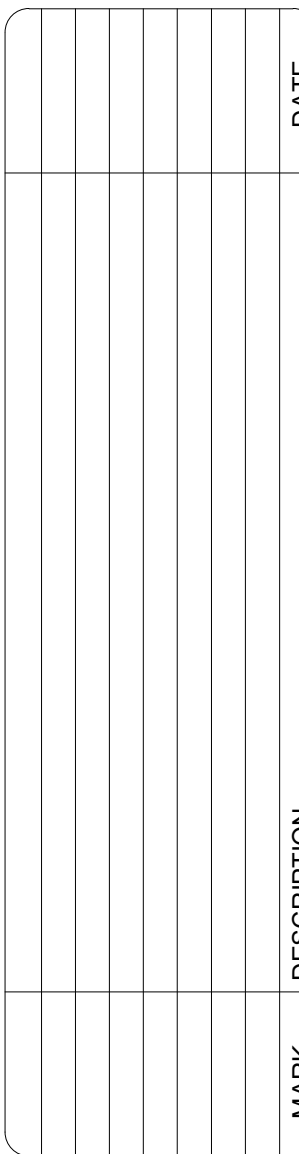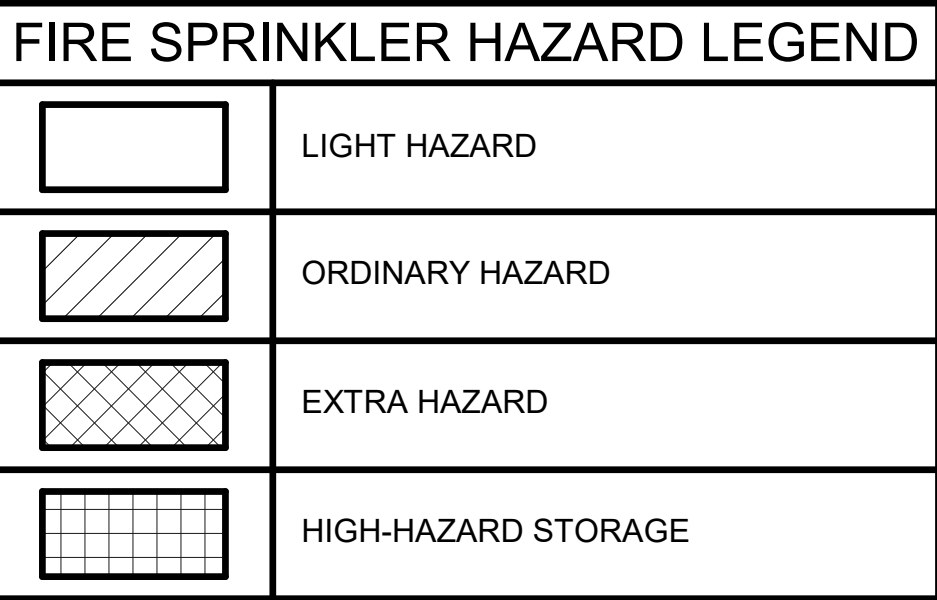


US ARMY CORPS OF ENGINEERS JAPAN ENGINEER DISTRICT KINAWA AREA OFFICE APO AP 96376-5132	DESIGNED BY: C. RUYNOY	ISSUE DATE:
DESIGN PARTNERS INCORPORATED 1350 KALANANU'U HIGHWAY, SUITE 1100 HONOLULU, HAWAII 96814	DRAWN BY: K. JERREKED BY: B. JIM ON	SOLICITATION NO.: CONTRACT NO.: W912HJ-17-D-0003
	SUBMITTED BY:	
	SIZE:	


FY20 MCA P177833 VEHICLE MAINTENANCE SHOP
KADENA AIR BASE, OKINAWA, JAPAN

SHEET ID

FXD111

INTERMEDIATE DESIGN

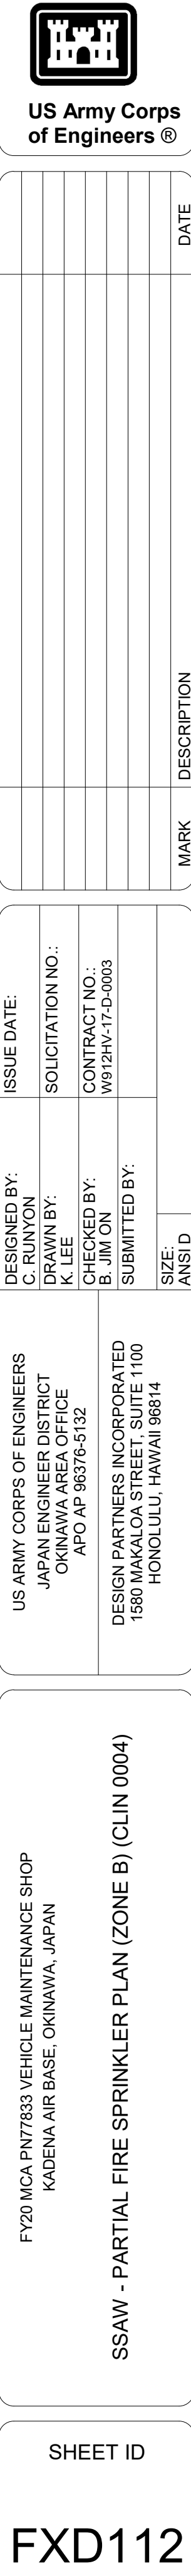

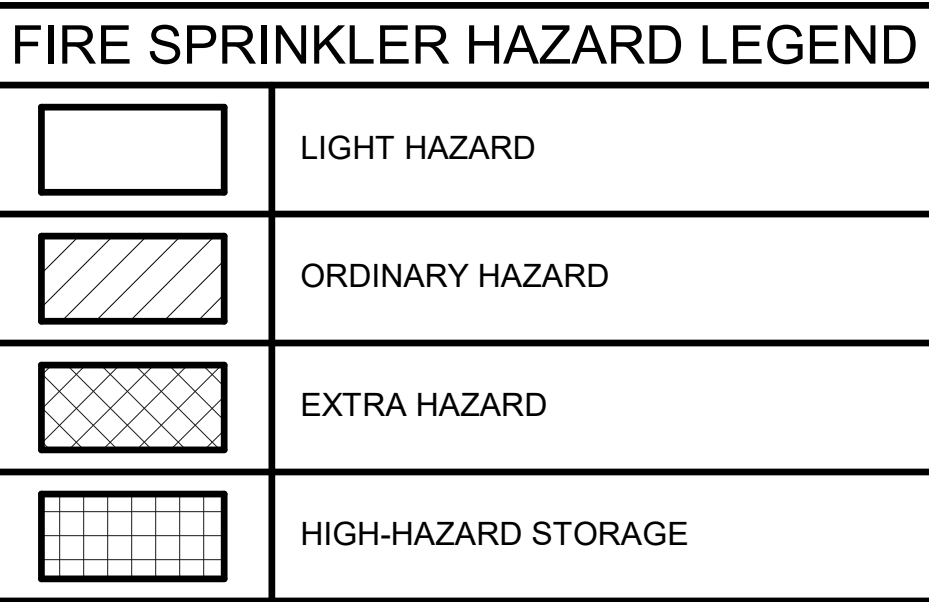
[illegible]

US ARMY CORPS OF ENGINEERS JAPAN ENGINEER DISTRICT KINAWA AREA OFFICE APO AP 96376-5132	DESIGNED BY: C. RUYNON	ISSUE DATE:
DESIGN PARTNERS INCORPORATED 1350 KALANANALANI BLVD. #1100 HONOLULU, HAWAII 96814	DRAWN BY: K. JERREKED BY: B. JIM ON	SOLICITATION NO.: CONTRACT NO.: W912HJ-17-D-0003
	SUBMITTED BY:	
	SIZE:	

FY20 MCA P177833 VEHICLE MAINTENANCE SHOP
KADENA AIR BASE, OKINAWA, JAPAN

SS - FIRE SPRINKLER PLAN (CLIN 0004)

SHEET ID
FX-E101

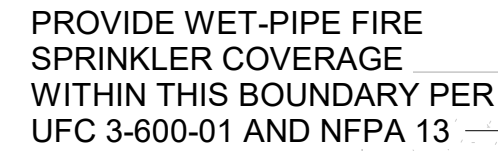


FIRE
PUMP
F101



SCALE: 1 : 50

GRAPHIC SCALE

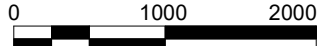

ALL DIMENSIONS AND/OR DIMENSIONS SHOWN IN
CALLOUT/ NOTES ARE IN MILLIMETERS UNLESS
OTHERWISE NOTED.

[illegible]


US ARMY CORPS OF ENGINEERS JAPAN ENGINEER DISTRICT OKINAWA AREA OFFICE APO AF 96376-5132	DESIGNED BY:	ISSUE DATE:
	C. RYUNOY K. YAMAWA K. YAMAWA	SOLICITATION NO.: CONTRACT NO.: W912HJV-17-D-0003
DESIGN PARTNERS INCORPORATED 1580 MAKALOA STREET, SUITE 1100 HONOLULU, HAWAII 96814	CHECKED BY:	
	B. JIM ON	SUBMITTED BY:
	SIZE:	ANSI/D


FY20 MCA PN77833 VEHICLE MAINTENANCE SHOP
KADENA AIR BASE, OKINAWA, JAPAN


FP - FIRE SPRINKLER PLAN (CLIN 0001)


SHEET ID

FX-F101

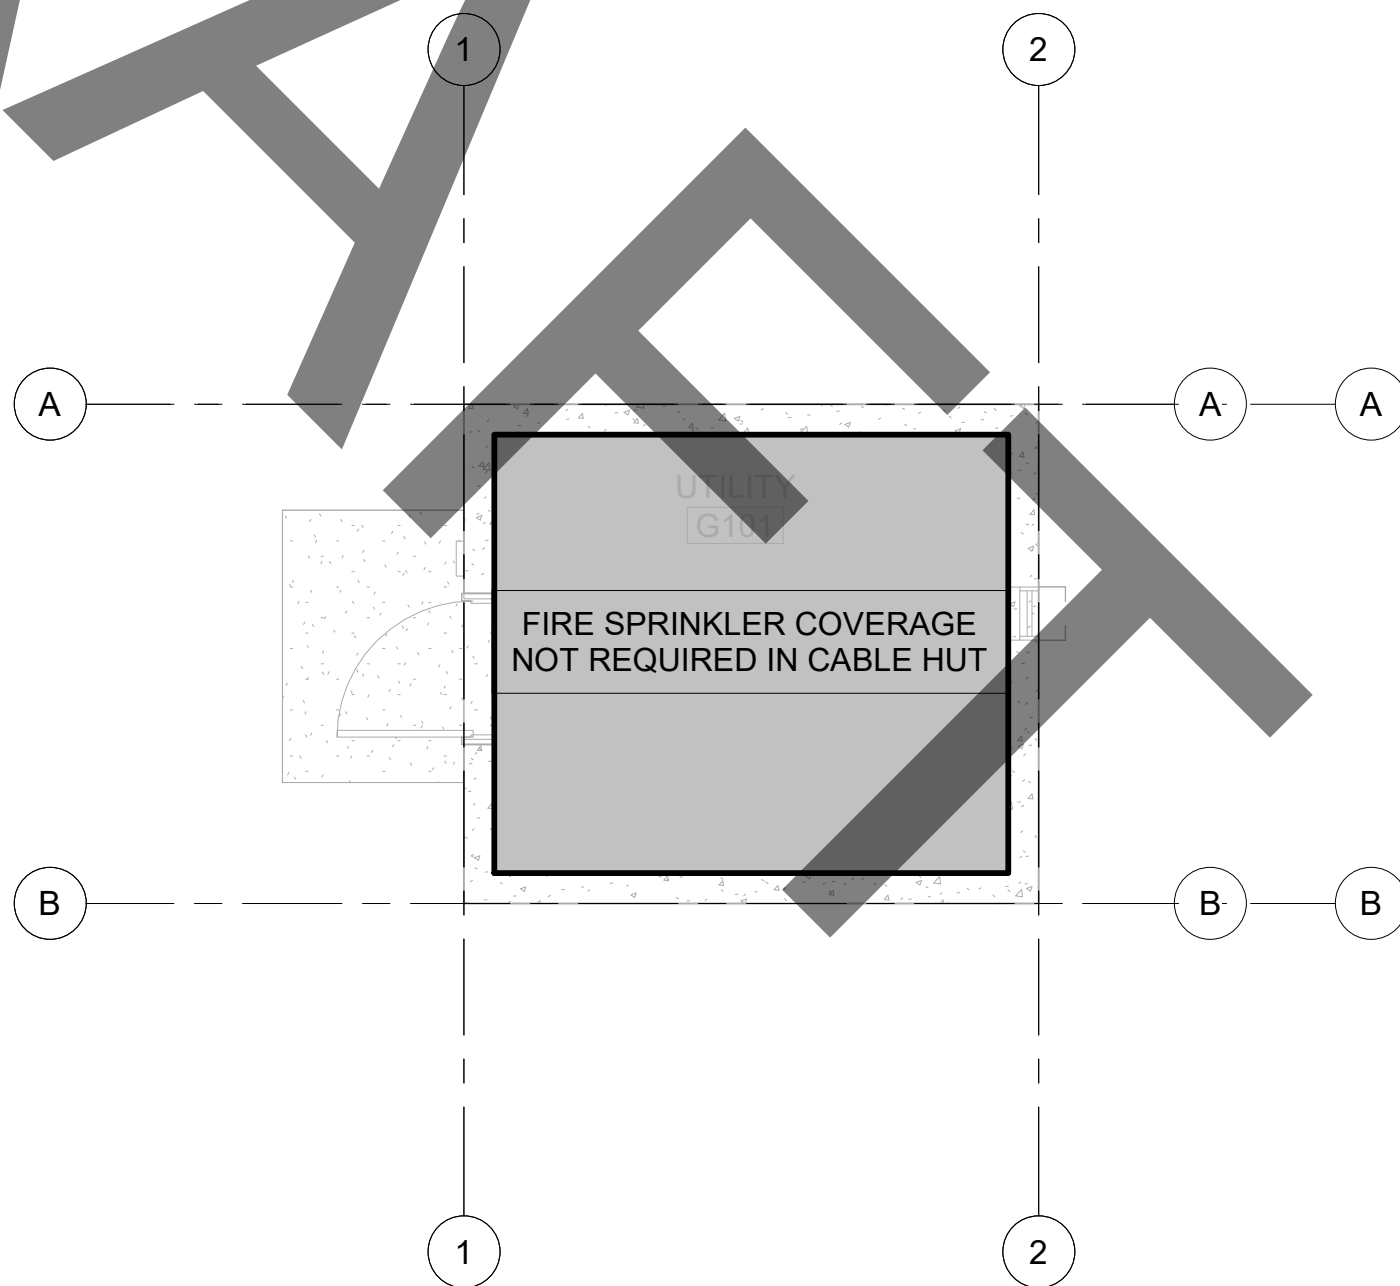

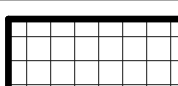FIRE SPRINKLER HAZARD LEGEND	
	LIGHT HAZARD
	ORDINARY HAZARD
	EXTRA HAZARD
	HIGH-HAZARD STORAGE

 US Army Corps of Engineers®			
SHEET ID		DATE	
FY20 MCA RW7893 VEHICLE MAINTENANCE SHOP KAGENA AIR BASE, OKINAWA, JAPAN		MARK	
CH - FIRE SPRINKLER PLAN (CLIN 0001)		DESCRIPTION	
US ARMY CORPS OF ENGINEERS JAPAN ENGINEER DISTRICT OKINAWA AREA OFFICE APO AP 96376-5132		ISSUE DATE:	
DESIGNED BY:		SOLICITATION NO.:	
DRAWN BY:		CONTRACT NO.:	
CHECKED BY:		W912HJV-17-D-0003	
SUBMITTED BY:		SIZE:	
DESIGN PARTNERS INCORPORATED 1580 MAKALOA STREET, SUITE 1100 HONOLULU, HAWAII 96814		ANSI D	

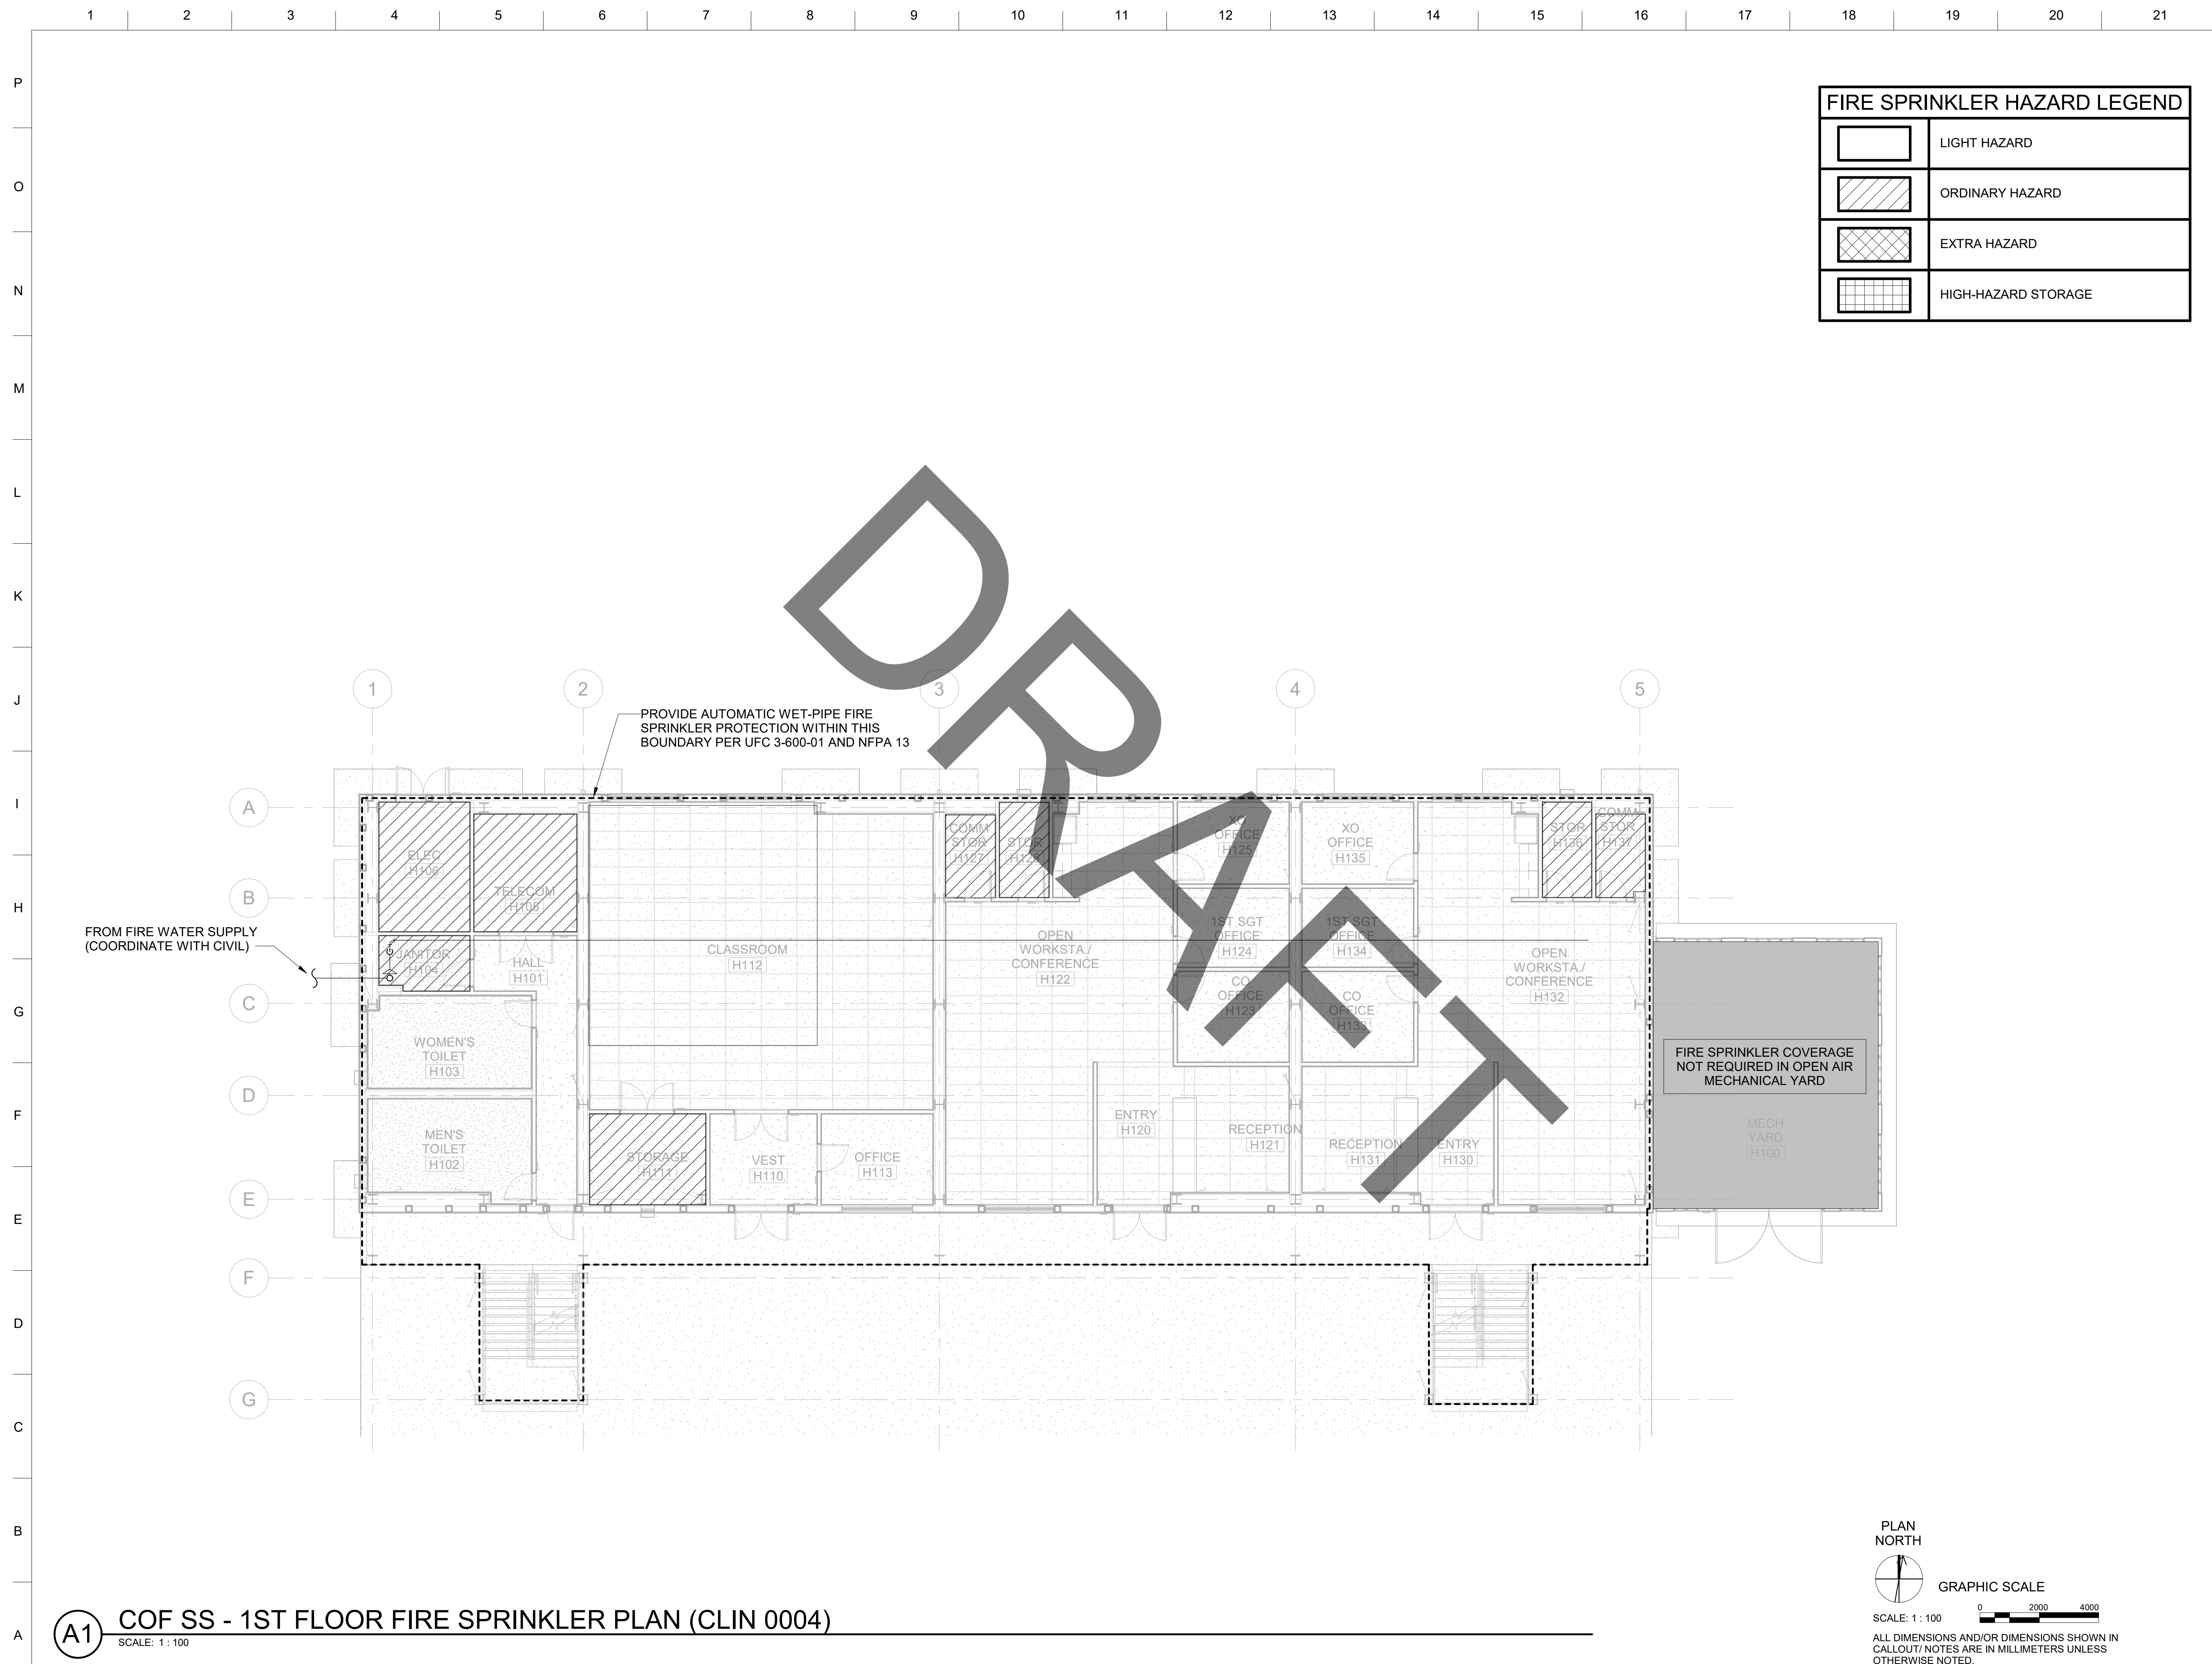

**US Army Corps
of Engineers ®**

[illegible]

U.S. ARMY CORPS OF ENGINEERS JAPAN ENGINEER DISTRICT OKINAWA AREA OFFICE APO AP 96376-5132	C. RYUNYON DRAWN BY: K. LEE	SOLICITATION NO.:
DESIGN PARTNERS, INCORPORATED 1580 MAKALOA STREET, SUITE 1100 HONOLULU, HAWAII 96814	CHECKED BY: O. CRABTREE	CONTRACT NO.:
	SUBMITTED BY: O. CRABTREE	W812HV-17-D-0003
	SIZE:	

FY20 MCA PN78333 VEHICLE MAINTENANCE SHOP
KADENA AIR BASE, OKINAWA, JAPAN


SHEET ID

FX-H101

INTERMEDIATE DESIGN

Plot Date: 12/16/2025 10:23:06 AM File Path:

C:\Users\Klee\Documents\511758_COF SS_FIRE_v2022_klee\MWXJU.rvt

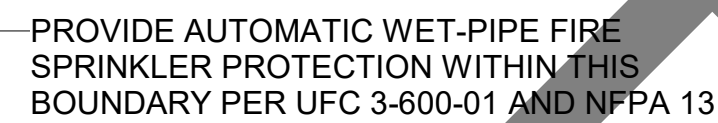

**US Army Corps
of Engineers®**

[illegible]

DESIGNED BY: I TSANG	ISSUE DATE:
DRAWN BY: JAPAN ENGINEER DISTRICT OKINAWA AREA OFFICE APO AP 96374-5132	CONTRACT NO.: W912HV-17-D-0003
CHECKED BY: O GRABTREE	SOLICITATION NO.:
SUBMITTED BY:	
SIZE: 11x17	

FY20 MCA PN7833 VEHICLE MAINTENANCE SHOP
KADENA AIR BASE, OKINAWA, JAPAN

SHEET ID

FX-H102

INTERMEDIATE DESIGN

Plot Date: 12/16/2025 10:23:07 AM File Path:

C:\Users\klee\Documents\511758_COF SS_FIRE_v2022_kleeMXXJU.rvt

PLAN
NORTH



GRAPHIC SCALE



ALL DIMENSIONS AND/OR DIMENSIONS SHOWN IN
CALLOUT/ NOTES ARE IN MILLIMETERS UNLESS
OTHERWISE NOTED.

COF SS - 2ND FLOOR FIRE SPRINKLER PLAN (CLIN 0004)


SCALE: 1 : 100


A
B
C
D
E
F
G
H
I
J
K
L
M
N
O
P

NAME	TYPE	CAPACITY LPM	PRESSURE KPA	POWER KW	VOLTAGE V	PHASE	HZ	START	STOP	REMARKS
FP 1	HORIZONTAL SPLIT CASE	5678	690	93.2	460	3	60	625 KPA	MANUAL	PROVIDE ALL ACCESSORIES TO MEET NFPA 20 AND SPECIFICATIONS 21 30 00. ALL ITEMS SHALL BE UL LISTED OR FM APPROVED.
JP 1	VERTICAL IN-LINE	38	760	1.9	460	3	60	660 KPA	730 KPA	PROVIDE ALL ACCESSORIES TO MEET NFPA 20 AND SPECIFICATIONS 21 30 00. ALL ITEMS SHALL BE UL LISTED OR FM APPROVED.

NAME	TYPE	SIZE (LITERS)
	INSULATED CONCRETE TANK	435,000 LITERS

- ① VALVE SHALL BE LOCATED 915MM A.F.F.
- ② VALVE SHALL BE LOCATED 1525MM A.F.F.
- ③ PIPING SHALL BE LOCATED 305MM BELOW FINISHED CEILING.

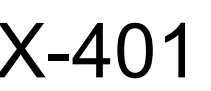

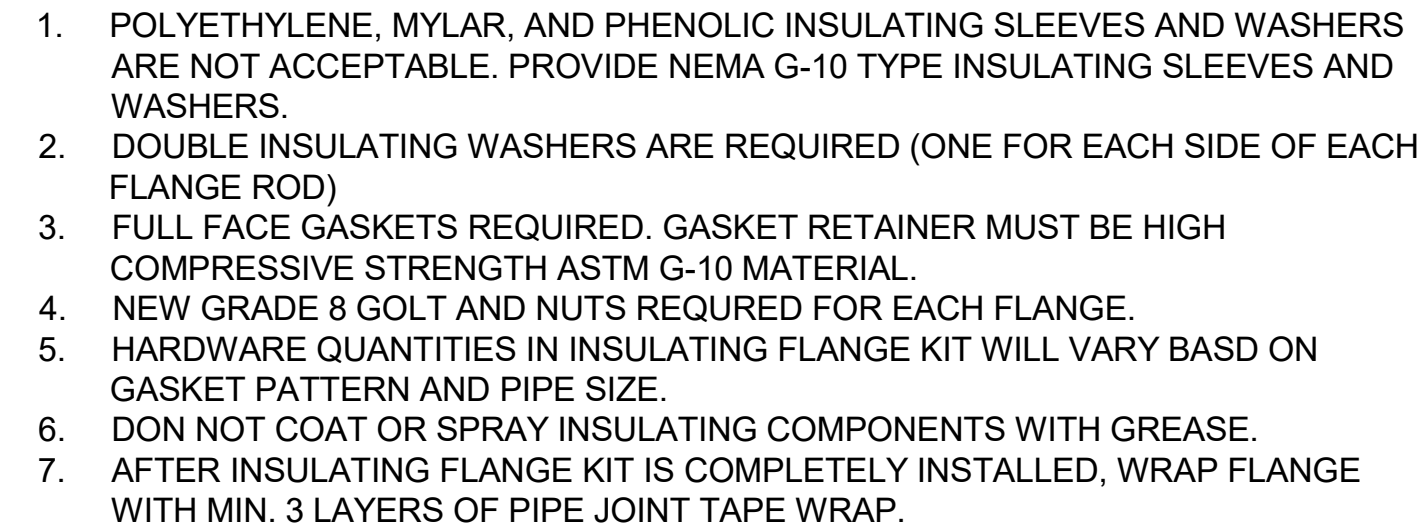

A14 DIELECTRIC INSULATING FLANGE
SCALE: NTS