



INSTALL ALTERNATE CONNECTIONS FOR STEAM AND CHILLED WATER

Department of Veterans Affairs Medical Center
VAMC - CAPE CORAL 2489 DIPLOMAT PKWY E., CAPE CORAL, FL 33909 PROJECT #: 516-22-602

ABOVE GROUP, INC.
MECHANICAL ELECTRICAL PLUMBING
305 EAST DRIVE, SUITE H
MELBOURNE, FL 32904
321.345.9026 P

RDC/JOHN POE ARCHITECTS
ARCHITECTURE
524 FERNWOOD DRIVE
ALTAMONTE SPRINGS, FL 32701
800.362.1523 P

DRUMMOND CARPENTER
CIVIL
47 EAST ROBINSON STREET, SUITE 210
ORLANDO, FL 32801
941.321.0924 P

STANTON ENGINEERING SERVICES, LLC
FIRE PROTECTION & LIFE SAFETY
10280 OLD COLUMBIA ROAD, SUITE 275
COLUMBIA, MD 21046
410.290.9301 P

OHC ENVIRONMENTAL
ENVIRONMENTAL
101 S. HOOVER BLVD., SUITE 101
TAMPA, FL 33609
813.626.8156 P


OCMI
COST ESTIMATING
2015 AYRSLY TOWN BLVD., SUITE 202
CHARLOTTE, NC 28273
704.280.8356 P



PROJECT LOCATION

SHEET LIST	
SHEET NUMBER	SHEET NAME
GENERAL	
G1001	COVER SHEET
AS101	ARCHITECTURAL SITE PLAN
STRUCTURAL	
S-001	GENERAL NOTES AND ABBREVIATIONS
SS101	FIRST FLOOR FOUNDATION AND SLAB ON GRADE PLAN
SS102	SECOND FLOOR FRAMING PLAN
S-301	DETAILS AND SECTIONS
MECHANICAL	
M-001	MECHANICAL NOTES, LEGENDS, & SYMBOLS
MS100	MECHANICAL SITE PLAN
MD101	FLOOR PLAN - MECHANICAL - DEMOLITION
MP101	FLOOR PLAN - MECHANICAL - NEW WORK
M-301	MECHANICAL SECTIONS
M-501	MECHANICAL DETAILS
M-502	MECHANICAL DETAILS
M-701	CHILLED WATER SYSTEM FLOW DIAGRAM
M-702	HEATING HOT WATER SYSTEM FLOW DIAGRAM
ELECTRICAL	
E-001	ELECTRICAL LEGENDS & SYMBOLS
E-002	ELECTRICAL GENERAL NOTES
EP101	FLOOR PLAN - ELECTRICAL - NEW WORK - LEVEL 1
EP102	FLOOR PLAN - ELECTRICAL - NEW WORK - LEVEL 2
E-501	ELECTRICAL DETAILS
E-601	ELECTRICAL DIAGRAMS

		CONSULTANT		ARCHITECT/ENGINEER OF RECORD		STAMP		Office of Construction and Facilities Management		Drawing Title COVER SHEET		Phase 100% CONSTRUCTION DOCUMENTS		Project Title INSTALL ALTERNATE CONNECTIONS FOR STEAM AND CHILLED WATER		Project Number 516-22-602	
										Approved:				Location CAPE CORAL VA		Drawing Number G1001	
												FULLY SPRINKLERED		Issue Date 08/07/2024		Checked ADL	
																Drawn JCP	

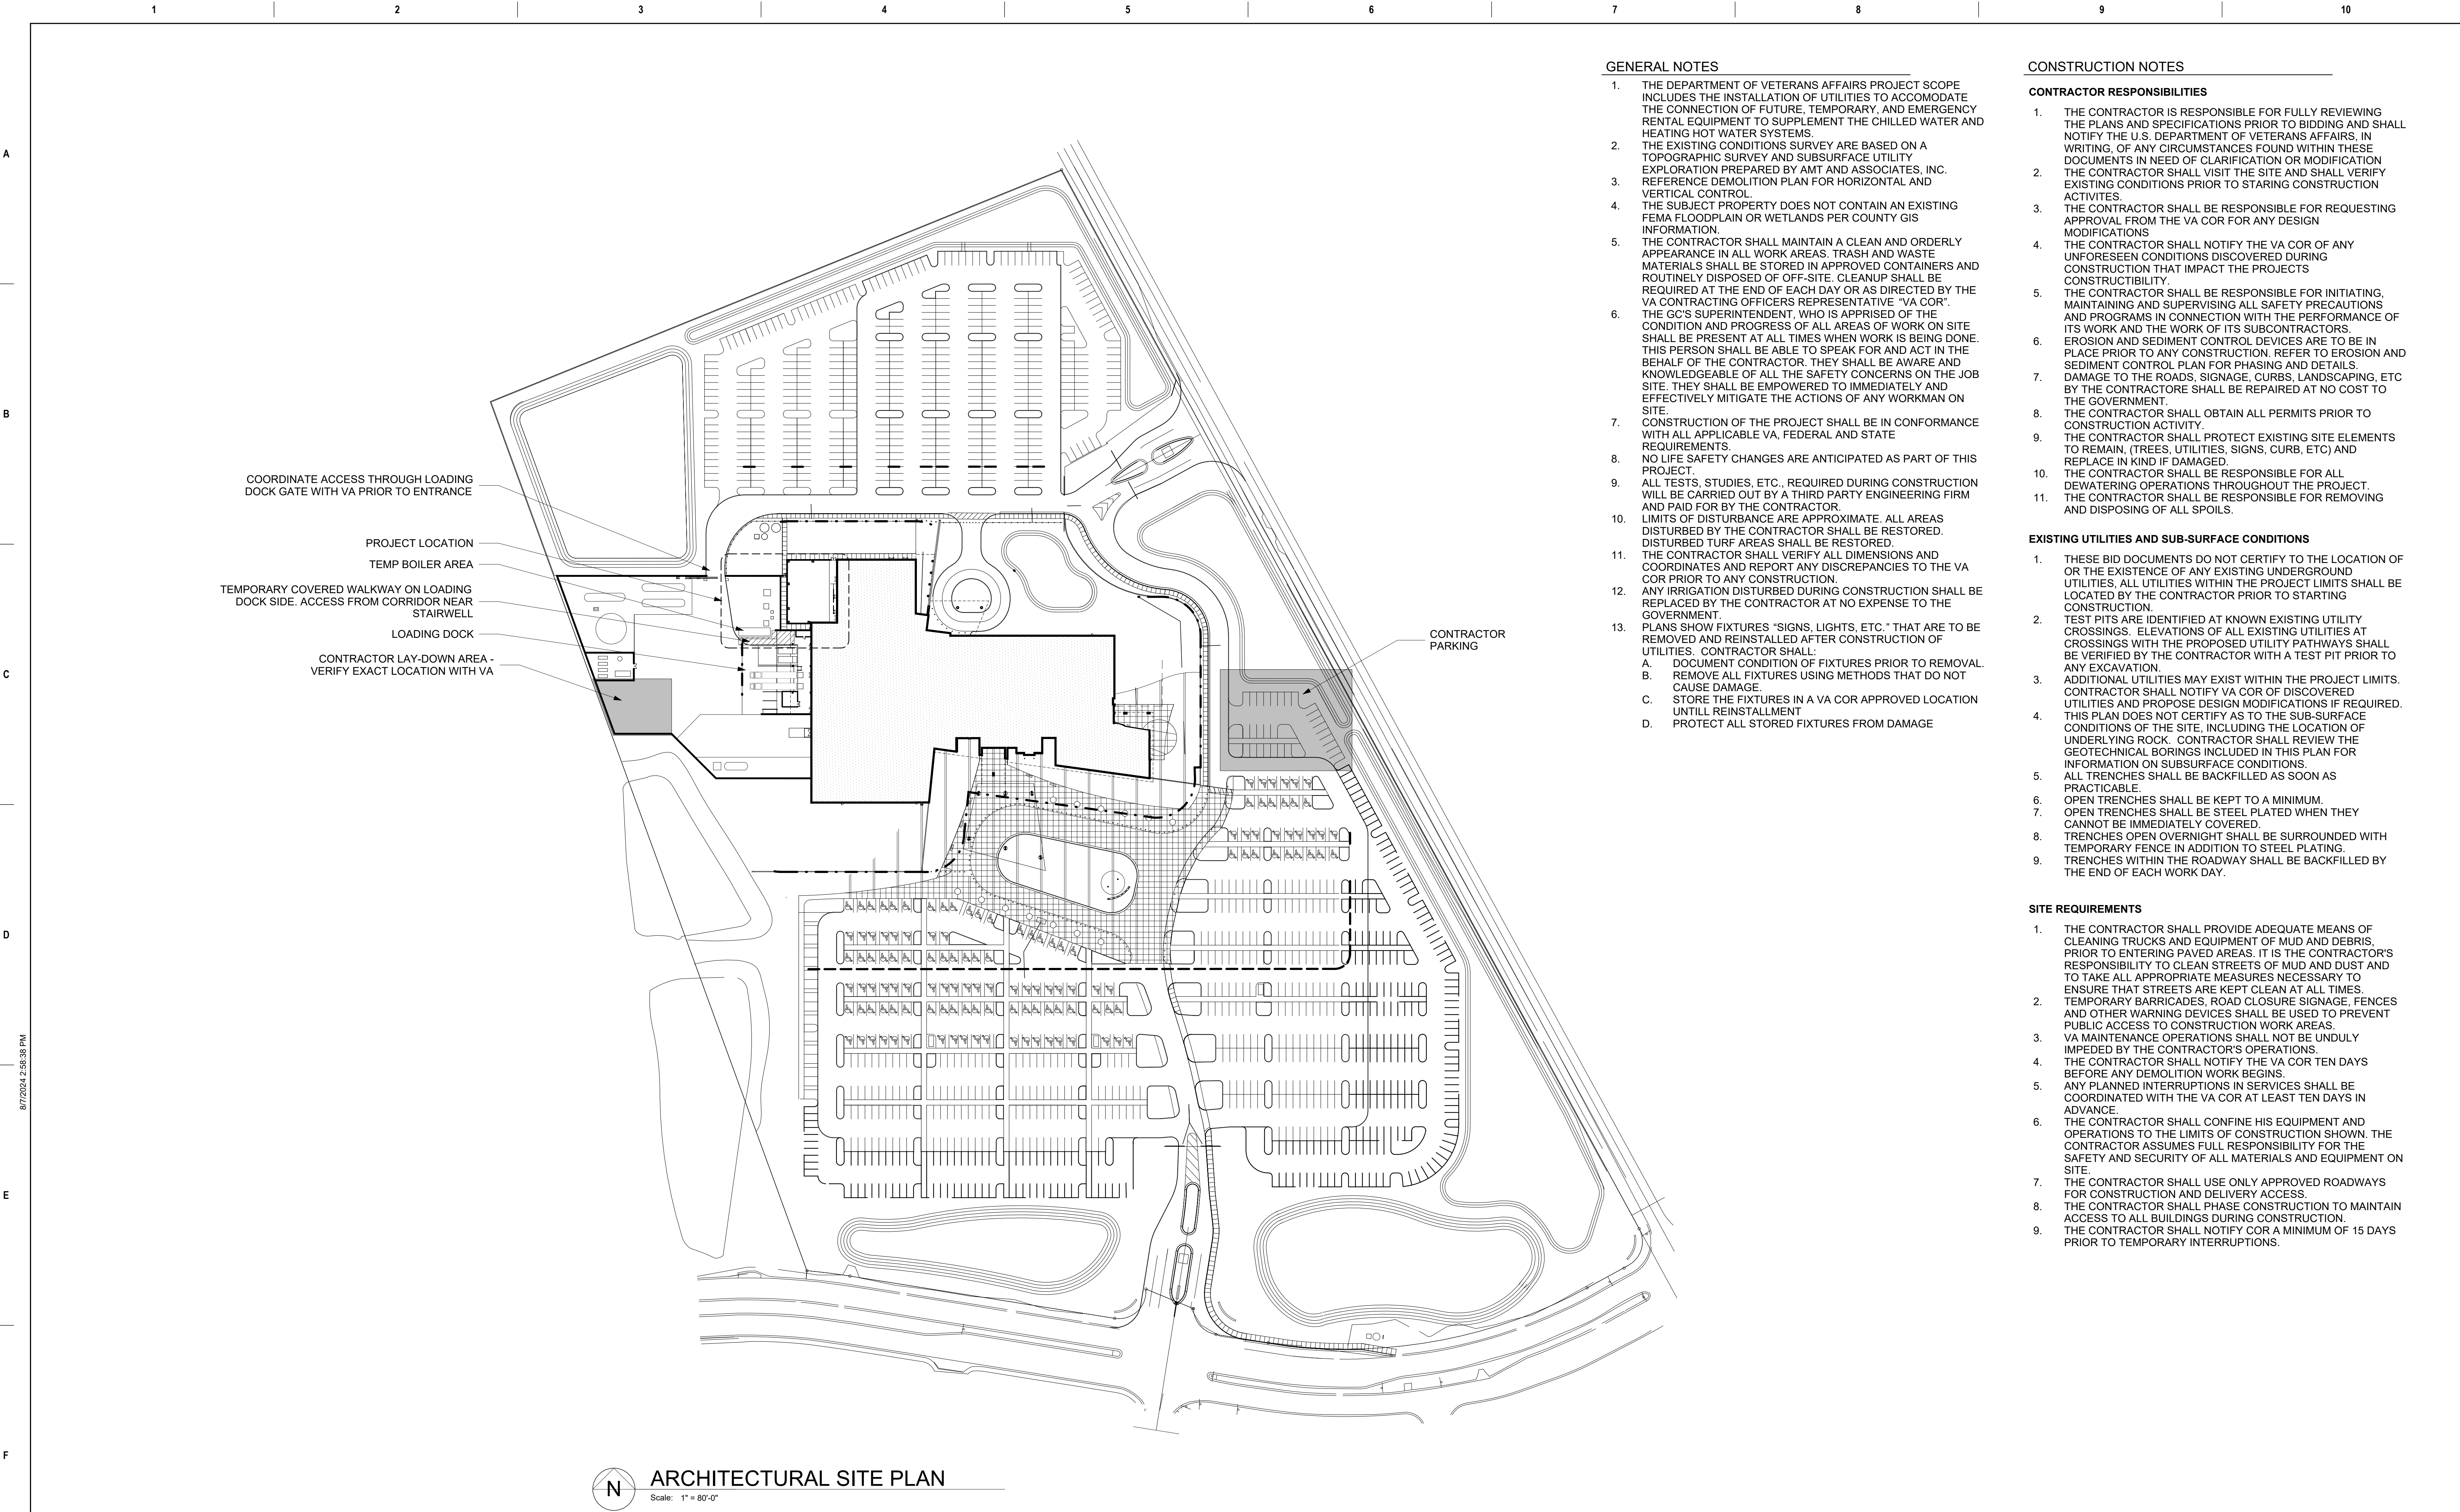

GENERAL NOTES

1. THE DEPARTMENT OF VETERANS AFFAIRS PROJECT SCOPE INCLUDES THE INSTALLATION OF UTILITIES TO ACCOMODATE THE CONNECTION OF FUTURE, TEMPORARY, AND EMERGENCY RENTAL EQUIPMENT TO SUPPLEMENT THE CHILLED WATER AND HEATING HOT WATER SYSTEMS.
2. THE EXISTING CONDITIONS SURVEY ARE BASED ON A TOPOGRAPHIC SURVEY AND SUBSURFACE UTILITY EXPLORATION PREPARED BY AMT AND ASSOCIATES, INC. REFERENCE DEMOLITION PLAN FOR HORIZONTAL AND VERTICAL CONTROL.
4. THE SUBJECT PROPERTY DOES NOT CONTAIN AN EXISTING FEMA FLOODPLAIN OR WETLANDS PER COUNTY GIS INFORMATION.
5. THE CONTRACTOR SHALL MAINTAIN A CLEAN AND ORDERLY APPEARANCE IN ALL WORK AREAS. TRASH AND WASTE MATERIALS SHALL BE STORED IN APPROVED CONTAINERS AND ROUTINELY DISPOSED OF OFF-SITE. CLEANUP SHALL BE REQUIRED AT THE END OF EACH DAY OR AS DIRECTED BY THE VA CONTRACTING OFFICERS REPRESENTATIVE "VA COR".
6. THE GC'S SUPERINTENDENT, WHO IS APPRISED OF THE CONDITION AND PROGRESS OF ALL AREAS OF WORK ON SITE SHALL BE PRESENT AT ALL TIMES WHEN WORK IS BEING DONE. THIS PERSON SHALL BE ABLE TO SPEAK FOR AND ACT IN THE BEHALF OF THE CONTRACTOR. THEY SHALL BE AWARE AND KNOWLEDGEABLE OF ALL THE SAFETY CONCERNS ON THE JOB SITE. THEY SHALL BE EMPOWERED TO IMMEDIATELY AND EFFECTIVELY MITIGATE THE ACTIONS OF ANY WORKMAN ON SITE.
7. CONSTRUCTION OF THE PROJECT SHALL BE IN CONFORMANCE WITH ALL APPLICABLE VA, FEDERAL AND STATE REQUIREMENTS.
8. NO LIFE SAFETY CHANGES ARE ANTICIPATED AS PART OF THIS PROJECT.
9. ALL TESTS, STUDIES, ETC., REQUIRED DURING CONSTRUCTION WILL BE CARRIED OUT BY A THIRD PARTY ENGINEERING FIRM AND PAID FOR BY THE CONTRACTOR.
10. LIMITS OF DISTURBANCE ARE APPROXIMATE. ALL AREAS DISTURBED BY THE CONTRACTOR SHALL BE RESTORED. DISTURBED TURF AREAS SHALL BE RESTORED.
11. THE CONTRACTOR SHALL VERIFY ALL DIMENSIONS AND COORDINATES AND REPORT ANY DISCREPANCIES TO THE VA COR PRIOR TO ANY CONSTRUCTION.
12. ANY IRRIGATION DISTURBED DURING CONSTRUCTION SHALL BE REPLACED BY THE CONTRACTOR AT NO EXPENSE TO THE GOVERNMENT.
13. PLANS SHOW FIXTURES "SIGNS, LIGHTS, ETC." THAT ARE TO BE REMOVED AND REINSTALLED AFTER CONSTRUCTION OF UTILITIES. CONTRACTOR SHALL:
 - A. DOCUMENT CONDITION OF FIXTURES PRIOR TO REMOVAL.
 - B. REMOVE ALL FIXTURES USING METHODS THAT DO NOT CAUSE DAMAGE.
 - C. STORE THE FIXTURES IN A VA COR APPROVED LOCATION UNTILL REINSTALLMENT
 - D. PROTECT ALL STORED FIXTURES FROM DAMAGE

CONSTRUCTION NOTES

CONTRACTOR RESPONSIBILITIES

1. THE CONTRACTOR IS RESPONSIBLE FOR FULLY REVIEWING THE PLANS AND SPECIFICATIONS PRIOR TO BIDDING AND SHALL NOTIFY THE U.S. DEPARTMENT OF VETERANS AFFAIRS, IN WRITING, OF ANY CIRCUMSTANCES FOUND WITHIN THESE DOCUMENTS IN NEED OF CLARIFICATION OR MODIFICATION
2. THE CONTRACTOR SHALL VISIT THE SITE AND SHALL VERIFY EXISTING CONDITIONS PRIOR TO STARING CONSTRUCTION ACTIVITES
3. THE CONTRACTOR SHALL BE RESPONSIBLE FOR REQUESTING APPROVAL FROM THE VA COR FOR ANY DESIGN MODIFICATIONS
4. THE CONTRACTOR SHALL NOTIFY THE VA COR OF ANY UNFORESEEN CONDITIONS DISCOVERED DURING CONSTRUCTION THAT IMPACT THE PROJECTS CONSTRUCTIBILITY
5. THE CONTRACTOR SHALL BE RESPONSIBLE FOR INITIATING, MAINTAINING AND SUPERVISING ALL SAFETY PRECAUTIONS AND PROGRAMS IN CONNECTION WITH THE PERFORMANCE OF ITS WORK AND THE WORK OF ITS SUBCONTRACTORS.
6. EROSION AND SEDIMENT CONTROL DEVICES ARE TO BE IN PLACE PRIOR TO ANY CONSTRUCTION. REFER TO EROSION AND SEDIMENT CONTROL PLAN FOR PHASING AND DETAILS.
7. DAMAGE TO THE ROADS, SIGNAGE, CURBS, LANDSCAPING, ETC BY THE CONTRACTORE SHALL BE REPAIRED AT NO COST TO THE GOVERNMENT.
8. THE CONTRACTOR SHALL OBTAIN ALL PERMITS PRIOR TO CONSTRUCTION ACTIVITY.
9. THE CONTRACTOR SHALL PROTECT EXISTING SITE ELEMENTS TO REMAIN, (TREES, UTILITIES, SIGNS, CURB, ETC) AND REPLACE IN KIND IF DAMAGED.
10. THE CONTRACTOR SHALL BE RESPONSIBLE FOR ALL DEWATERING OPERATIONS THROUGHOUT THE PROJECT.
11. THE CONTRACTOR SHALL BE RESPONSIBLE FOR REMOVING AND DISPOSING OF ALL SPOILS.

EXISTING UTILITIES AND SUB-SURFACE CONDITIONS

1. THESE BID DOCUMENTS DO NOT CERTIFY TO THE LOCATION OF OR THE EXISTENCE OF ANY EXISTING UNDERGROUND UTILITIES. ALL UTILITIES WITHIN THE PROJECT LIMITS SHALL BE LOCATED BY THE CONTRACTOR PRIOR TO STARTING CONSTRUCTION.
2. TEST PITS ARE IDENTIFIED AT KNOWN EXISTING UTILITY CROSSINGS. ELEVATIONS OF ALL EXISTING UTILITIES AT CROSSINGS WITH THE PROPOSED UTILITY PATHWAYS SHALL BE VERIFIED BY THE CONTRACTOR WITH A TEST PIT PRIOR TO ANY EXCAVATION.
3. ADDITIONAL UTILITIES MAY EXIST WITHIN THE PROJECT LIMITS. CONTRACTOR SHALL NOTIFY VA COR OF DISCOVERED UTILITIES AND PROPOSE DESIGN MODIFICATIONS IF REQUIRED. THIS PLAN DOES NOT CERTIFY AS TO THE SUB-SURFACE CONDITIONS OF THE SITE, INCLUDING THE LOCATION OF UNDERLYING ROCK. CONTRACTOR SHALL REVIEW THE GEOTECHNICAL BORINGS INCLUDED IN THIS PLAN FOR INFORMATION ON SUBSURFACE CONDITIONS.
5. ALL TRENCHES SHALL BE BACKFILLED AS SOON AS PRACTICABLE.
6. OPEN TRENCHES SHALL BE KEPT TO A MINIMUM.
7. OPEN TRENCHES SHALL BE STEEL PLATED WHEN THEY CANNOT BE IMMEDIATELY COVERED.
8. TRENCHES OPEN OVERNIGHT SHALL BE SURROUNDED WITH TEMPORARY FENCE IN ADDITION TO STEEL PLATING.
9. TRENCHES WITHIN THE ROADWAY SHALL BE BACKFILLED BY THE END OF EACH WORK DAY.

SITE REQUIREMENTS

1. THE CONTRACTOR SHALL PROVIDE ADEQUATE MEANS OF CLEANING TRUCKS AND EQUIPMENT OF MUD AND DEBRIS. PRIOR TO ENTERING PAVED AREAS. IT IS THE CONTRACTOR'S RESPONSIBILITY TO CLEAN STREETS OF MUD AND DUST AND TO TAKE ALL APPROPRIATE MEASURES NECESSARY TO ENSURE THAT STREETS ARE KEPT CLEAN AT ALL TIMES.
2. TEMPORARY BARRICADES, ROAD CLOSURE SIGNAGE, FENCES AND OTHER WARNING DEVICES SHALL BE USED TO PREVENT PUBLIC ACCESS TO CONSTRUCTION WORK AREAS.
3. VA MAINTENANCE OPERATIONS SHALL NOT BE UNDULY IMPEDED BY THE CONTRACTOR'S OPERATIONS.
4. THE CONTRACTOR SHALL NOTIFY THE VA COR TEN DAYS BEFORE ANY DEMOLITION WORK BEGINS.
5. ANY PLANNED INTERRUPTIONS IN SERVICES SHALL BE COORDINATED WITH THE VA COR AT LEAST TEN DAYS IN ADVANCE.
6. THE CONTRACTOR SHALL CONFINE HIS EQUIPMENT AND OPERATIONS TO THE LIMITS OF CONSTRUCTION SHOWN. THE CONTRACTOR ASSUMES FULL RESPONSIBILITY FOR THE SAFETY AND SECURITY OF ALL MATERIALS AND EQUIPMENT ON SITE.
7. THE CONTRACTOR SHALL USE ONLY APPROVED ROADWAYS FOR CONSTRUCTION AND DELIVERY ACCESS.
8. THE CONTRACTOR SHALL PHASE CONSTRUCTION TO MAINTAIN ACCESS TO ALL BUILDINGS DURING CONSTRUCTION.
9. THE CONTRACTOR SHALL NOTIFY COR A MINIMUM OF 15 DAYS PRIOR TO TEMPORARY INTERRUPTIONS.

	</
--	--	----

A

B

C

D

E

F

8/6/2024 4:32:21 PM

AutoSave Docs\10123047 - VA Cape Coral Alt. Connections\0123047 - Cape Coral Alt. Connections - R22_5.rvt

GENERAL NOTES

GENERAL:	FOUNDATIONS:	POST-INSTALLED ANCHORS:
1. CONTRACTOR IS SOLELY RESPONSIBLE FOR MEANS AND METHODS DURING THE COURSE OF THE WORK. DO NOT DAMAGE EXISTING OR ENDANGER THE STRUCTURAL INTEGRITY OF THE WORK.	1. FOUNDATIONS ARE DESIGNED FOR A BEARING PRESSURE OF 3000 PSF. THE WORK SHALL BE IN ACCORDANCE WITH THE SPECIFICATIONS OF ARDAMAN & ASSOCIATES, INC. JOB NUMBER 08-4522 IN REPORT DATED JULY 30, 2008.	1. DRILL AND INSTALL POST-INSTALLED ANCHORS ACCORDING TO MANUFACTURER'S PRINTED INSTALLATION INSTRUCTIONS AND PER MANUFACTURER'S ON-SITE TRAINING.
2. THE BUILDING FRAME IS NOT SELF-SUPPORTING UNTIL THE ENTIRE STRUCTURAL SYSTEM HAS BEEN INSTALLED. TEMPORARY BRACING MUST BE PROVIDED BY THE CONTRACTOR TO SUPPORT THE FRAME UNTIL THE STRUCTURAL SYSTEM HAS BEEN COMPLETED.	2. CONTRACTOR SHALL NOTIFY THE GEOTECHNICAL ENGINEER FOR INSPECTION BEFORE PLACING ANY FOOTINGS. GEOTECHNICAL ENGINEER SHALL INSPECT AND REPORT ON ADEQUACY OF BEARING MATERIAL.	2. ALL INSTALLERS OF POST-INSTALLED ANCHORS SHALL BE ACI/CRSI ADHESIVE ANCHOR INSTALLER CERTIFIED. SUBMIT CERTIFICATES FOR RECORD.
3. NOTIFY COR IN CASE OF DISCREPANCIES BETWEEN DRAWINGS, THESE NOTES, AND PROJECT MANUAL BEFORE PROCEEDING WITH THE WORK.	3. FOOTINGS SHOULD BE CAST ON THE SAME DAY IN WHICH EXCAVATION FOR THEM IS COMPLETED. IF PLACING OF CONCRETE IS DELAYED, FOOTING BOTTOM SHALL BE TRIMMED TO FIRM MATERIAL IMMEDIATELY BEFORE CASTING.	3. ALL POST-INSTALLED ANCHORS SHALL MEET ICC-ES COMPLIANCE FOR EACH TYPE OF APPLICATION.
4. USE ARCHITECTURAL DRAWINGS AND DRAWINGS OF OTHER TRADES IN CONJUNCTION WITH THE STRUCTURAL DRAWINGS TO PROPERLY PERFORM THE WORK.	4. PLACE CONCRETE IN DRY EXCAVATIONS ONLY. NOTE SOIL AND WATER CONDITIONS AS SHOWN BY BORINGS AND DEPTHS OF FOOTINGS AS SHOWN ON FOUNDATION PLANS. PENDING APPROVAL BY THE COR, CONTRACTOR MAY ELECT TO CONDUCT FURTHER SUBSURFACE INVESTIGATIONS AT THEIR OWN EXPENSE.	4. SUBMIT PRODUCT INFORMATION AND ICC-ES EVALUATION REPORT FOR EACH ANCHOR.
5. IF CONDITIONS DISCLOSED DURING EXCAVATION REVEAL UNFORESEEN CONDITIONS, PROMPTLY REQUEST DIRECTION FROM COR BEFORE PROCEEDING.	5. FOOTINGS SHALL BE FORMED UNLESS OTHERWISE PERMITTED BY THE ENGINEER.	5. ALL ANCHOR DESIGNS ARE FOR INSTALLATION IN THE FOLLOWING CONDITIONS, UNLESS NOTED OTHERWISE. WRITTEN APPROVAL MUST BE RECEIVED FROM ENGINEER PRIOR TO INSTALLATION OF ADHESIVE ANCHORS IN ALTERNATE CONDITIONS. A. DRY CONCRETE, UNLESS NOTED OTHERWISE. B. CONCRETE TEMPERATURE AT TIME OF INSTALLATION MUST BE BETWEEN 14° F AND 104° F. SEE MANUFACTURER'S PRINTED INSTALLATION INSTRUCTION FOR ADHESIVE GEL AND CURE TIMES. C. ANCHOR HOLES TO BE HAMMER DRILLED. D. ANCHOR HOLES TO BE CLEANED PER MANUFACTURER'S PRINTED INSTALLATION INSTRUCTIONS PRIOR TO ADHESIVE INJECTION. E. ANCHORS/POST-INSTALLED REINFORCING SHALL NOT BE LOADED UNTIL CONCRETE OR GROUT HAS BEEN ALLOWED TO CURE FOR 21 DAYS AND/OR HAS ATTAINED 70% OF ITS DESIGN STRENGTH.
6. CONTRACTOR IS RESPONSIBLE FOR COORDINATING BETWEEN TRADES.	6. STRUCTURAL FILL INCLUDING UNDER FOOTINGS: A. SHALL BE PLACED IN MINIMUM OF 12" LOOSE LIFT THICKNESS AND COMPACTED TO 95% OF STANDARD PROCTOR. B. ON-SITE OR IMPORTED GRANULAR FILL INCLUDING SW, SP, SM, SO CLASSIFIED IN ACCORDANCE WITH THE UNIFIED SOIL CLASSIFICATION SYSTEM (USCS) AND WITHIN 2% OF OPTIMUM MOISTURE. FURTHERMORE, THE MATERIAL TO BE UTILIZED AS STRUCTURAL FILL SHOULD HAVE LESS THAN 12% PASSING THE U.S. NO. 200 SIEVE.	6. ALL POST-INSTALLED ANCHORS IN CONCRETE SHALL BE SUITED FOR USE IN SEISMIC AND CRACKED CONCRETE APPLICATIONS.
7. DO NOT SCALE DRAWINGS.	7. FILL UNDER SLABS ON GRADE SHALL BE COMPACTED TO 98% OF STANDARD PROCTOR DENSITY. TESTS SHALL BE PERFORMED FOR EACH LIFT.	7. ADHESIVE ANCHORS IN CONCRETE SHALL BE HLTI HIT HY-200, OR APPROVED EQUAL.
8. FIELD DIMENSIONS: IF STRUCTURAL DRAWINGS ARE USED FOR LAYING OUT COLUMN CENTERS AND WALL LINES, ALL DIMENSIONS SHALL FIRST BE VERIFIED WITH THE ARCHITECTURAL AND MEP DRAWINGS. LAYOUT SHALL BE CHECKED BEFORE WORK IS BEGIN.	8. PREPARATION OF SUBGRADES FOR TEMPORARY TRAILERS SHALL BE 12" COMPACTED GRAVEL PER THE ORIGINAL GEOTECHNICAL REPORT AS FOLLOWS: "LIMEROCK OR SHELL-ROCK COMPACTED TO AT LEAST 98% OF THE MODIFIED PROCTOR MAXIMUM DRY DENSITY (AASHTO-18) AND IN ACCORDANCE WITH FOOT SECTION 200. MATERIAL USED AS BASE COURSE SHOULD CONFORM TO FOOT SECTION 911 OR 913A REQUIREMENTS. MINIMUM LIMEROCK BEARING RATIO OF 100%."	8. ADHESIVE ANCHORS IN MASONRY AND HOLLOW CMU SHALL BE HLTI HIT HY-270 WITH MESH SLEEVES, OR APPROVED EQUAL.
9. SECTIONS AND DETAILS SHOWN, WHILE DRAWN FOR SPECIFIC LOCATIONS, ARE INTENDED TO ESTABLISH THE GENERAL TYPES OF DETAILS WILL APPLY TO OTHER LOCATIONS.	9. REPRODUCTION OF CONTRACT DOCUMENTS WILL NOT BE ACCEPTED AS SHOP DRAWINGS.	9. EXPANSION ANCHORS IN CONCRETE SHALL BE HLTI Kwik Bolt T2Z, OR APPROVED EQUAL.
10. THE ENGINEER'S REVIEW OF A SUBMITTAL SHALL NOT RELIEVE THE CONTRACTOR OF THEIR RESPONSIBILITY TO FOLLOW THE INTENT OF THE CONTRACT DRAWINGS.	10. THE CONTRACTOR SHALL PREPARE AND SUBMIT TO THE COR FOR REVIEW A SITE SPECIFIC RIGGING AND HOISTING PLAN FOR ALL MAJOR EQUIPMENT THAT WILL BE TRANSPORTED THROUGH OR HOISTED FROM THE BUILDING. THE PLAN SHALL INCLUDE THE SEQUENCE OF ERECTION, THE DESCRIPTION OF THE RIGGING, HOISTING AND TRANSPORTATION EQUIPMENT AND THE SITE PREPARATIONS THAT WILL BE NEEDED TO COMPLETE THE INSTALLATION.	10. PROVIDE STANDARD AISI C HOLES IN ALL STEEL MEMBERS RECEIVING POST-INSTALLED ANCHORS. IF OVERSIZED HOLES ARE PROVIDED TO EASE INSTALLATION OF THE ANCHORS, A PLATE WASHER (14"x2"x2") WITH AN AISI STANDARD HOLE SHALL BE INSTALLED AND 18" FILLET WELDED (ALL AROUND) TO THE MEMBER.
11. REPRODUCTION OF CONTRACT DOCUMENTS WILL NOT BE ACCEPTED AS SHOP DRAWINGS.	11. ALL CONCRETE EXPOSED TO THE WEATHER SHALL BE f'c=5000 PSI MINIMUM AND SHALL BE AIR ENTRAINED FOR EXPOSURE CLASS F2 PER ACI 318 "BUILDING CODE REQUIREMENTS FOR STRUCTURAL CONCRETE".	11. ALL ANCHORS AND REINFORCING SHALL BE INSTALLED IN ACCORDANCE WITH THE SPACING AND EDGE DISTANCES SHOWN IN THE DRAWINGS. THE CONTRACTOR SHALL INFORM THE ARCHITECT PRIOR TO INSTALLING THE ANCHORS IF THE SPACING AND EDGE DISTANCES SHOWN IN THE DRAWINGS CANNOT BE ACHIEVED. IF THIS IS THE CASE, RE-DESIGN MIGHT BE REQUIRED AND THE ANCHORS SHOULD NOT BE INSTALLED UNTIL APPROVAL HAS BEEN PROVIDED BY THE ENGINEER.
	12. DO NOT CUT ANY REINFORCING UNLESS IT IS SPECIFICALLY INDICATED IN THE DRAWINGS OR IS APPROVED BY THE ENGINEER.	12. DO NOT CUT ANY REINFORCING UNLESS IT IS SPECIFICALLY INDICATED IN THE DRAWINGS OR IS APPROVED BY THE ENGINEER.
	13. POST INSTALLED ANCHORS AND REINFORCING SHALL ONLY BE USED WHERE SPECIFIED IN THE CONTRACT DRAWINGS. THE CONTRACTOR SHALL OBTAIN APPROVAL FROM THE ENGINEER PRIOR TO INSTALLING POST INSTALLED ANCHORS WHERE CAST-IN PLACE ANCHORS ARE MISSING, MISPLACED OR DAMAGED.	13. POST INSTALLED ANCHORS AND REINFORCING SHALL ONLY BE USED WHERE SPECIFIED IN THE CONTRACT DRAWINGS. THE CONTRACTOR SHALL OBTAIN APPROVAL FROM THE ENGINEER PRIOR TO INSTALLING POST INSTALLED ANCHORS WHERE CAST-IN PLACE ANCHORS ARE MISSING, MISPLACED OR DAMAGED.
	14. "WARNING" PRECAST CONCRETE PANELS MAY HAVE PRESTRESSED STRANDS. SERIOUS HAZARDOUS DAMAGE CAN RESULT FROM A STRAND BEING CUT. GPR SCANNING OF PRECAST CONCRETE WALLS IS REQUIRED PRIOR TO INSTALLING POST-INSTALLED ANCHORS. NO REINFORCING SHALL BE CUT. HOLES OR ANCHORS WILL NEED TO BE RELOCATED.	14. "WARNING" PRECAST CONCRETE PANELS MAY HAVE PRESTRESSED STRANDS. SERIOUS HAZARDOUS DAMAGE CAN RESULT FROM A STRAND BEING CUT. GPR SCANNING OF PRECAST CONCRETE WALLS IS REQUIRED PRIOR TO INSTALLING POST-INSTALLED ANCHORS. NO REINFORCING SHALL BE CUT. HOLES OR ANCHORS WILL NEED TO BE RELOCATED.
		15. ALL EXPOSED STEEL SHALL BE HOT-DIPPED GALVANIZED.

STRUCTURAL ABBREVIATIONS

ABBR.	DESCRIPTION	ABBR.	DESCRIPTION	ABBR.	DESCRIPTION
AB	ANCHOR BOLT	ES	EACH SIDE	OC	ON CENTER
ABV	ABOVE	EXCAV	EXCAVATE/EXCAVATION	OD	OUTSIDE DIAMETER
ACI	AMERICAN CONCRETE INSTITUTE	EXP	EXPANSION	OF	OUTSIDE FACE
ADOL	ADDITIONAL	EXT	EXTERIOR	O-O	OUT-TO-OUT
ADH	ADHESIVE	EXIST	EXISTING	OPG	OPENING
ADJ	ADJACENT, ADJUSTMENT	EW	EACH WAY	OPP	OPPOSITE
AESS	ARCHITECT/ENGINEER	F	FACE OF	OSB	ORIENTED STRAND BOARD
AFF	ABOVE FINISHED FLOOR	FAB	FABRICATE	OSHA	OCCUPATIONAL SAFETY AND HEALTH ADMINISTRATION
AGG	AGGREGATE	FB	FLAT BAR	OSL	OUTSTANDING LEG
AHJ	AUTHORITY HAVING JURISDICTION	FBO	FURNISHED BY OTHERS	OSL	ORIENTED STRAND LUMBER
AISC	AMERICAN INSTITUTE OF STEEL CONSTRUCTION	FDN	FOUNDATION	OVS	OVERSIZED HOLE
AISI	AMERICAN IRON AND STEEL INSTITUTE	FFE	FINISHED FLOOR ELEVATION		
AISC 341-16	SEISMIC PROVISIONS FOR STRUCTURAL STEEL BUILDINGS	FIN	FINISHED		
		FL(R)	FLOOR	PAF	POWDER ACTUATED FASTENER
		FLG	FLANGE	PC	PRECAST CONCRETE, PIECE
		FND	FOUNDATION	PCF	POUNDS PER CUBIC FOOT
		FO	FACE OF	PEB	PERESTIAL
		FOC	FACE OF CONCRETE	PERP	PERPENDICULAR
		FOP	FACE OF FINISH	PREFAB	PREFABRICATE(D)
		FOM	FACE OF MASONRY	PL	PLATE
		FOS	FACE OF STUD	PLF	POUNDS PER LINEAR FOOT
		FP	FIREPROOFING	PLYWD	PLYWOOD
		FRMG	FRAMING	PMF	PREMOULDED FILLER
		FRP	FIBER-REINFORCED POLYMER	PROJ	PROJECTION
		FRT	FIRE RETARDANT TREATED	PSF	POUNDS PER SQUARE FOOT
		FS	FAR SIDE	PSI	POUNDS PER SQUARE INCH
		FT	FEET	PSL	PARALLEL STRAND LUMBER
		FTG	FOOTING	PT	PRESERVATIVE-TREATED, POST-TENSIONED
		FUT	FUTURE	PVC	POLYVINYL CHLORIDE
		FV	FIELD VERIFY	QTY	QUANTITY
		GA	GAUGE	R	RADIUS
		GALV	GALVANIZED	RCMU	REINFORCED CONCRETE MASONRY UNIT
		GB	GRADE BEAM	RCSC	RESEARCH COUNCIL ON STRUCTURAL CONNECTIONS
		GC	GENERAL CONTRACTOR	RD	ROOF DECK
		GLB	GLUE LAMINATED BEAM	REF	REFERENCE
		GR	GRADE	RFR	REINFORCED/REINFORCEMENT
		GYP	GYPSUM	REQ(Q)	REQUIRED
				RET	RETAINING
		HD	HEAVY DUTY	RGR	ROUGH OPENING
		HDR	HEADER	RGMT(S)	ROUGH OPENING REQUIREMENT(S)
		HEF	HORIZONTAL EACH FACE	RTO	ROUGH OPENING
		HGR	HANGER	RUN	ROUGH OPENING
		HI	HIGH		
		HIF	HORIZONTAL INSIDE FACE		
		HOK	HORIZONTAL OUTSIDE FACE		
		HOF	HORIZONTAL OUTSIDE FACE		
		HORIZ	HORIZONTAL		
		HP	HIGH POINT		
		HS	HIGH STRENGTH		
		HT	HEIGHT		
		HV	HORIZONTAL & VERTICAL		
		HVAC	HEATING, VENTILATING & AIR CONDITIONING		
				BC	INTERNATIONAL BUILDING COUNCIL
		IC	INTERNATIONAL CODE COUNCIL	CC	INTERNATIONAL CODE COUNCIL
		ID	INSIDE DIAMETER	CD	INTERNATIONAL CODE COUNCIL
		IE	INSIDE FACE	IC	INTERNATIONAL CODE COUNCIL
		IFC	ISSUE FOR CONSTRUCTION	IS	INTERNATIONAL CODE COUNCIL
		IN	INCH	IS	INTERNATIONAL CODE COUNCIL
		IND	INCLUDING(D)	IS	INTERNATIONAL CODE COUNCIL
		INFO	INFORMATION	IS	INTERNATIONAL CODE COUNCIL
		INSTL	INSTALLATION	IS	INTERNATIONAL CODE COUNCIL
		INSUL	INSULATION	IS	INTERNATIONAL CODE COUNCIL
		INT	INTERIOR	IS	INTERNATIONAL CODE COUNCIL
		INT	INVERT(ED)	IS	INTERNATIONAL CODE COUNCIL
		JOIST(S)	JOIST(S)	IS	INTERNATIONAL CODE COUNCIL
		JOINT	JOINT	IS	INTERNATIONAL CODE COUNCIL
		K	KIP (THOUSAND POUNDS)	IS	INTERNATIONAL CODE COUNCIL
		KNEE BRACE	KNEE BRACE	IS	INTERNATIONAL CODE COUNCIL
		KPS	KIPS PER SQUARE INCH	IS	INTERNATIONAL CODE COUNCIL
				IS	INTERNATIONAL CODE COUNCIL
		LB #	POUND LEADER (BOARD)	IS	INTERNATIONAL CODE COUNCIL
		LDGR	LEDGER (BOARD)	IS	INTERNATIONAL CODE COUNCIL
		LEN	LENGTH	IS	INTERNATIONAL CODE COUNCIL
		LP	LONG	IS	INTERNATIONAL CODE COUNCIL
		LL	LIVE LOAD	IS	INTERNATIONAL CODE COUNCIL
		LLBB	LONG LEGS BACK TO BACK	IS	INTERNATIONAL CODE COUNCIL
		LLH	LONG LEG HORIZONTAL	IS	INTERNATIONAL CODE COUNCIL
		LLV	LONG LEG VERTICAL	IS	INTERNATIONAL CODE COUNCIL
		LOCN	LOCATION	IS	INTERNATIONAL CODE COUNCIL
		LONGIT	LONGITUDINAL	IS	INTERNATIONAL CODE COUNCIL
		LP	LOW POINT	IS	INTERNATIONAL CODE COUNCIL
		LRFD	LOAD AND RESISTANCE FACTOR DESIGN	IS	INTERNATIONAL CODE COUNCIL
		LSD	LONG SLOTTED HOLE	IS	INTERNATIONAL CODE COUNCIL
		LVL	LAMINATED VENEER LUMBER	IS	INTERNATIONAL CODE COUNCIL
		LW	LONG WAY	IS	INTERNATIONAL CODE COUNCIL
		LWC	LIGHT WEIGHT CONCRETE	IS	INTERNATIONAL CODE COUNCIL
				IS	INTERNATIONAL CODE COUNCIL
		M	MOMENT	IS	INTERNATIONAL CODE COUNCIL
		MAS	MASONRY	IS	INTERNATIONAL CODE COUNCIL
		MATL	MATERIAL	IS	INTERNATIONAL CODE COUNCIL
		MAX	MAXIMUM	IS	INTERNATIONAL CODE COUNCIL
		MECH	MECHANICAL	IS	INTERNATIONAL CODE COUNCIL
		MEP	MECHANICAL, ELECTRICAL & PLUMBING	IS	INTERNATIONAL CODE COUNCIL
		MEZZ	MEZZANINE	IS	INTERNATIONAL CODE COUNCIL
		MFR	MANUFACTURER	IS	INTERNATIONAL CODE COUNCIL
		MIN	MINIMUM	IS	INTERNATIONAL CODE COUNCIL
		MISC	MISCELLANEOUS	IS	INTERNATIONAL CODE COUNCIL
		MO	MASONRY OPENING	IS	INTERNATIONAL CODE COUNCIL
		MONO	MONOLITHIC	IS	INTERNATIONAL CODE COUNCIL
		MPH	MILES PER HOUR	IS	INTERNATIONAL CODE COUNCIL
		MTL	METAL	IS	INTERNATIONAL CODE COUNCIL
				IS	INTERNATIONAL CODE COUNCIL
		(E)	EXISTING	IS	INTERNATIONAL CODE COUNCIL
		E	EAST	IS	INTERNATIONAL CODE COUNCIL
		EA	EACH	IS	INTERNATIONAL CODE COUNCIL
		EF	EACH FACE	IS	INTERNATIONAL CODE COUNCIL
		EFS	EXTERIOR INSULATION FINISH SYSTEM	IS	INTERNATIONAL CODE COUNCIL
		EJ	EXPANSION JOINT	IS	INTERNATIONAL CODE COUNCIL
		EL	ELEVATION	IS	INTERNATIONAL CODE COUNCIL
		ELEC	ELECTRICAL	IS	INTERNATIONAL CODE COUNCIL
		ELEV	ELEVATION	IS	INTERNATIONAL CODE COUNCIL
		EMBED	EMBEDMENT/EMBEDDED	IS	INTERNATIONAL CODE COUNCIL
		ENGR	ENGINEER	IS	INTERNATIONAL CODE COUNCIL
		EO	EDGE OF DECK	IS	INTERNATIONAL CODE COUNCIL
		EOD	EDGE OF DECK	IS	INTERNATIONAL CODE COUNCIL
		EOM	EDGE OF MASONRY	IS	INTERNATIONAL CODE COUNCIL
		EOS	EDGE OF SLAB	IS	INTERNATIONAL CODE COUNCIL
		EQ	EQUAL	IS	INTERNATIONAL CODE COUNCIL
		EQUIP	EQUIPMENT	IS	INTERNATIONAL CODE COUNCIL
		ES	EACH SIDE	IS	INTERNATIONAL CODE COUNCIL


CONSULTANT

ARCHITECT/ENGINEER OF RECORD



www.abovegroupinc.com
COA/CA Lic. No. 31120

305 East Dr., Suite H,
Melbourne, Florida 32904
PH: 321.345.9026

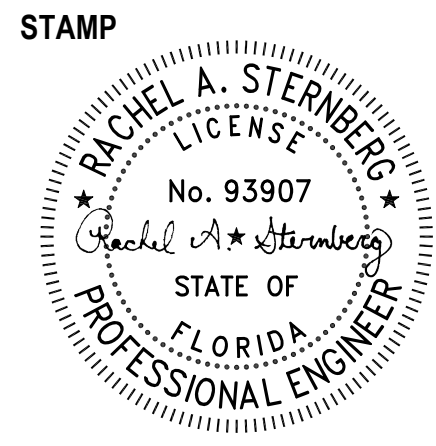

Office of
Construction
and Facilities
Management

VA U.S. Department of
Veterans Affairs

Drawing Title
**GENERAL NOTES AND
ABBREVIATIONS**

Approved:

Phase
**100% CONSTRUCTION
DOCUMENTS**

FULLY SPRINKLERED

Project Title
**INSTALL ALTERNATE
CONNECTIONS FOR STEAM
AND CHILLED WATER**

Location
CAPE CORAL VA

Issue Date
08/07/2024

Checked
RAS

Drawn
SLS

Project Number
516-22-602

Building Number

Drawing Number

S-001

SHEET LIST


Sheet Number	Sheet Name
S-001	GENERAL NOTES AND ABBREVIATIONS
SS101	FIRST FLOOR FOUNDATION AND SLAB ON GRADE PLAN
SS102	SECOND FLOOR FRAMING PLAN
S-301	DETAILS AND SECTIONS

DRAWING NOTES:


1. EXISTING CONDITIONS SHOWN ARE BASED ON ORIGINAL CONSTRUCTION DOCUMENTS AND A LIMITED AMOUNT OF FIELD OBSERVATION. CONTRACTOR TO VERIFY DIMENSIONS PRIOR TO CUTTING HOLES IN WALLS OR FABRICATING STEEL.
2. TOP OF STEEL IS NOTED THUS, () ON PLAN FROM LEVEL 1.
3. **WARNING:** PRECAST CONCRETE PANELS MAY HAVE PRESTRESSED STRANDS. SERIOUS HAZARDS CAN RESULT FROM A STRAND BEING HIT. GPR SCANNING OF PRECAST CONCRETE AND CMU WALLS IS REQUIRED PRIOR TO CUTTING HOLES IN WALLS, INSTALLING POST-INSTALLED ANCHORS, OR FABRICATING STEEL. NO REINFORCING SHALL BE CUT. IF REINFORCING IS OBSERVED IN THE LOCATION OF THE PROPOSED HOLE OR ANCHOR, IT WILL NEED TO BE RELOCATED.

CODED NOTES:

1. PREPARE SUBGRADE FOR TEMPORARY EMENTION. PROVIDE 12" MIN. COMPACTED GRAVEL. REFER TO GENERAL NOTES FOR FURTHER DIRECTION.
2. PREPARE FORMS FOR CURBSIDE OF 4'-0" TO 4'-6" PIPE COLUMNS AND 2'-0" x 4'-0" x 1'-6" FOOTING WITH 4 #6 LWP TOP & BOTTOM AND #6 SW TOP & BOTTOM.
3. UNSTRAUCH CHANNEL SUPPORT TO EXISTING PRECAST CONCRETE PANEL. COORDINATE LOCATION AND ELEVATION WITH ELECTRICAL DRAWINGS.
4. PENETRATION IN EXISTING PRECAST PANEL. COORDINATE SIZE AND LOCATION WITH MECHANICAL AND ELECTRICAL DRAWINGS.
5. PENETRATION IN EXISTING 6" CMU WALL. COORDINATE SIZE AND LOCATION WITH MECHANICAL AND ELECTRICAL DRAWINGS.
6. (a) (3) 12x16x16" ANGLES (LVL) WITH 3/8" BOLT PANEL EXTEND 6" PAST EDGE OF OPENING. REFER TO DETAIL 2, S-301.
7. ELECTRICAL CONDUIT. REFER TO ELECTRICAL DRAWINGS.
8. HOT WATER PIPES. REFER TO MECHANICAL DRAWINGS.
9. COLD WATER PIPES. REFER TO MECHANICAL DRAWINGS.

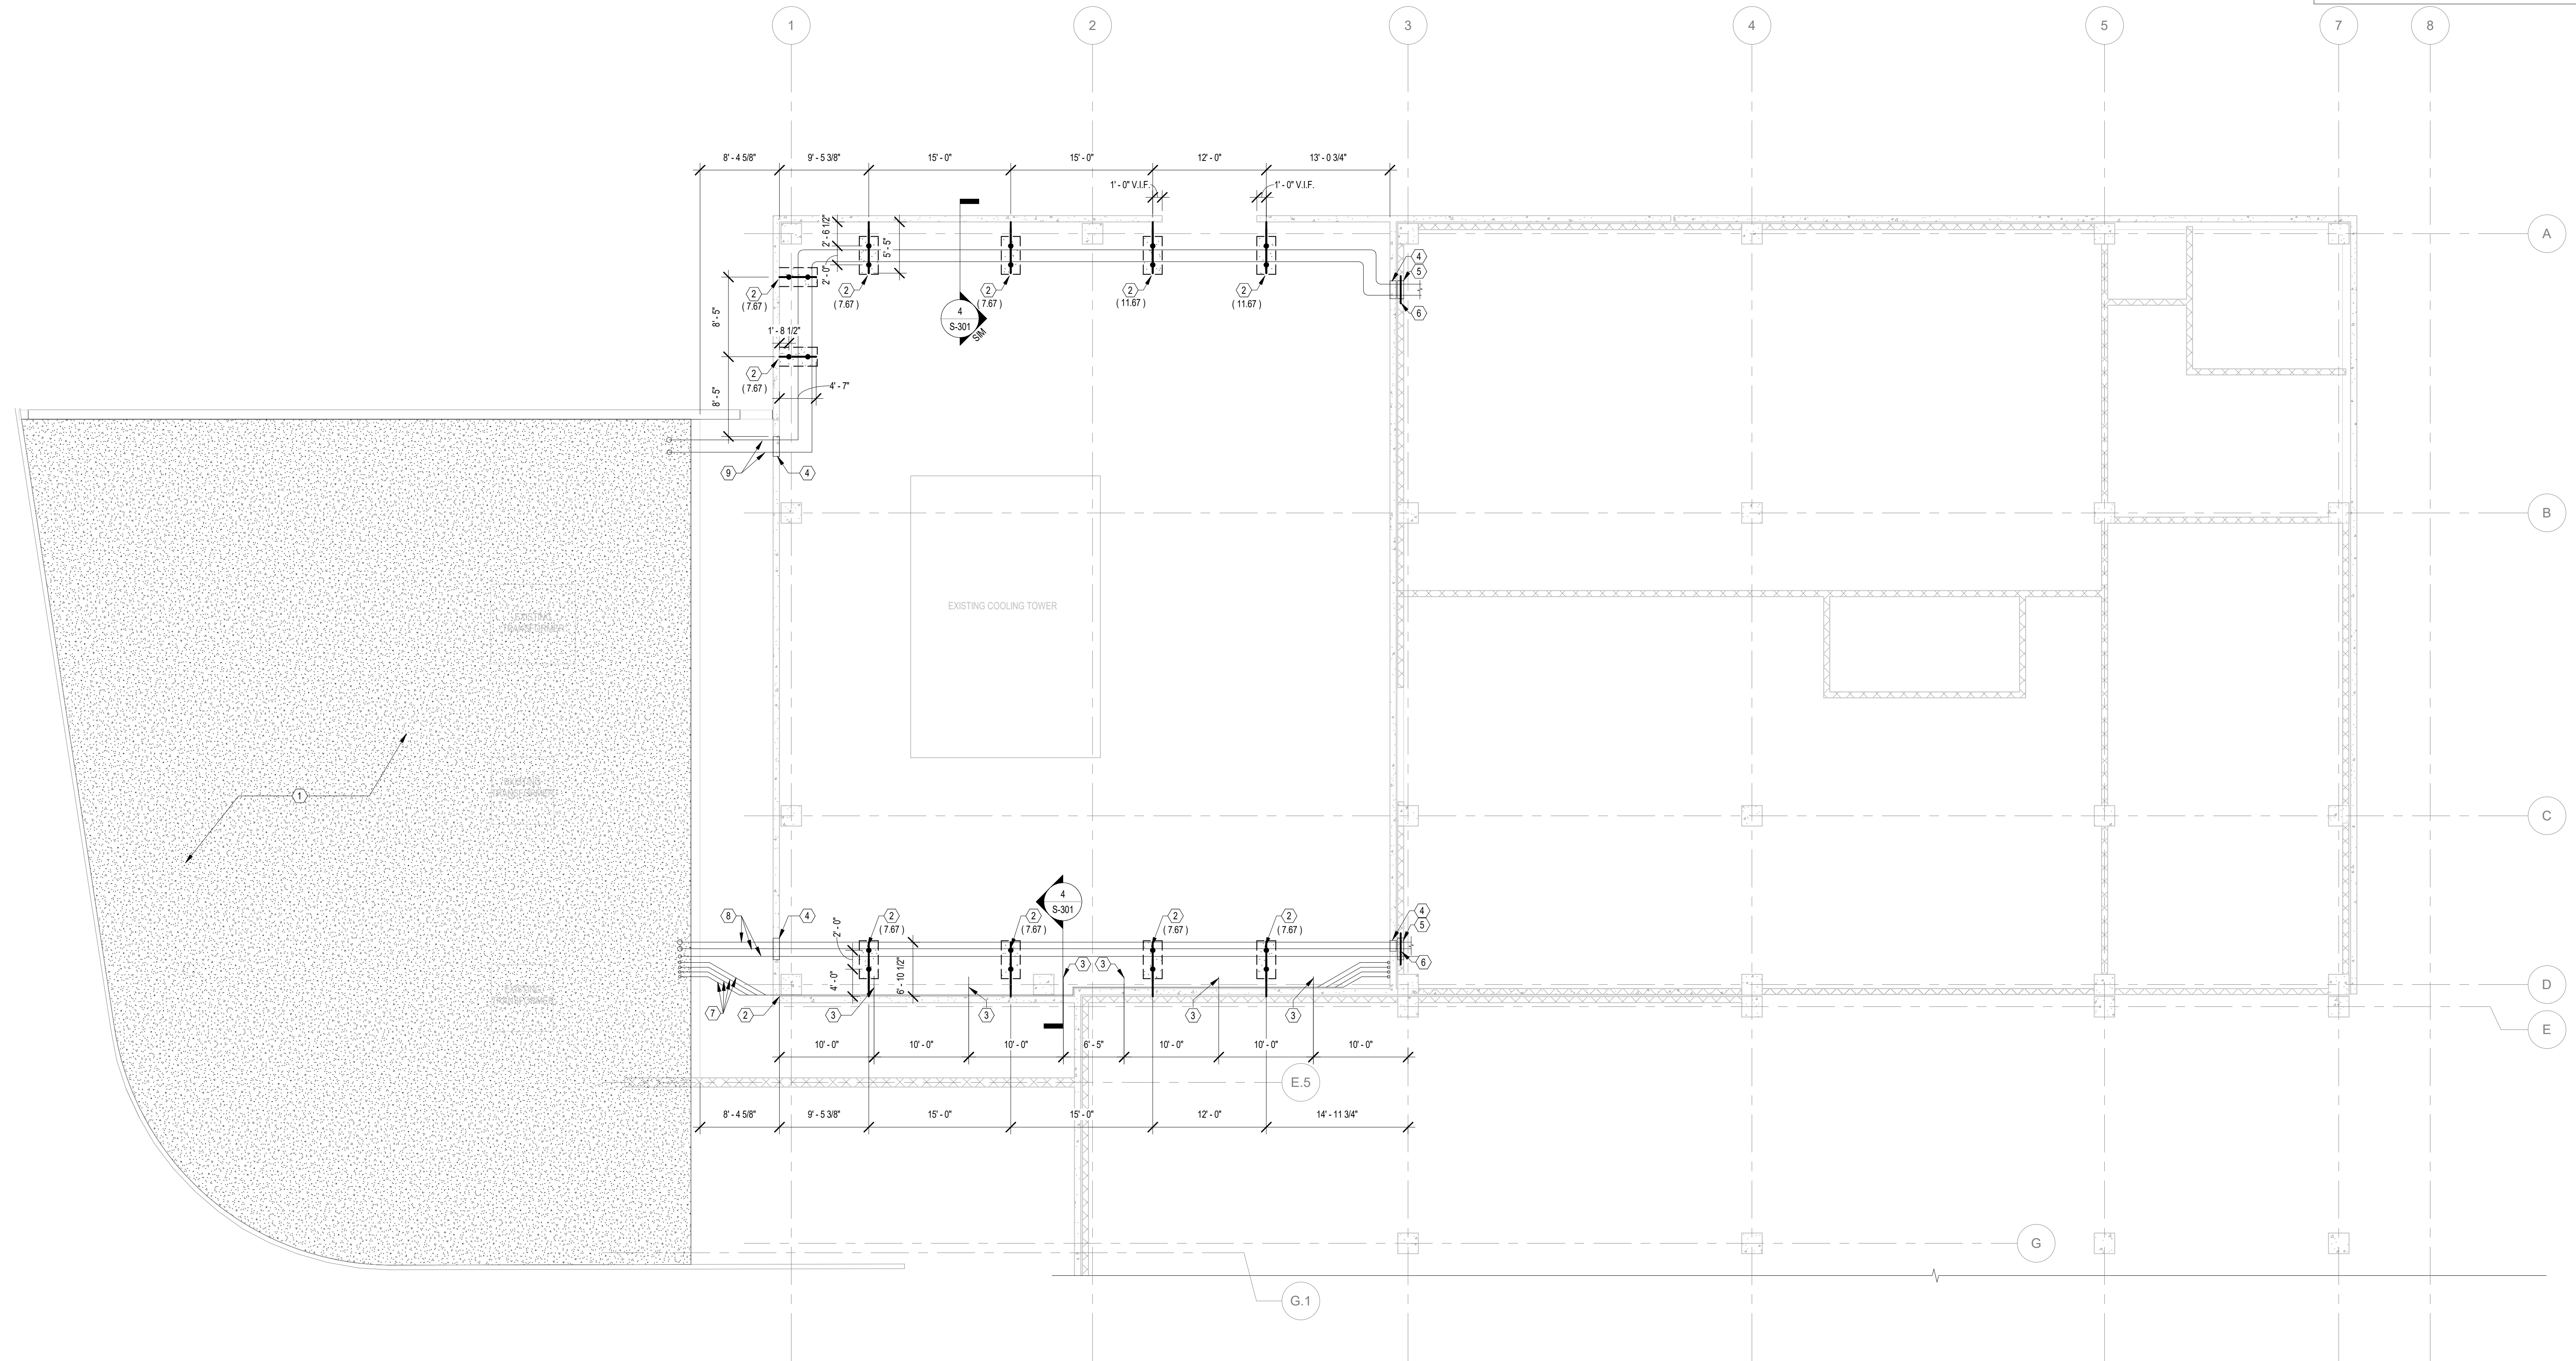


1 FIRST FLOOR FOUNDATION AND SLAB ON GRADE PLAN
1/8" = 1'-0"

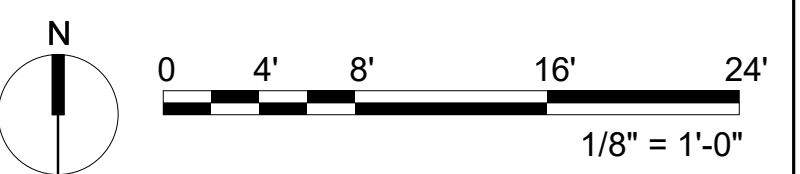[illegible]





- DRAWING NOTES:**
- EXISTING CONDITIONS SHOWN ARE BASED ON ORIGINAL CONSTRUCTION DOCUMENTS AND A LIMITED AMOUNT OF FIELD OBSERVATION. CONTRACTOR TO VERIFY DIMENSIONS PRIOR TO CUTTING HOLES IN WALLS OR FABRICATING STEEL.
 - WARNING:** PRECAST CONCRETE PANELS MAY HAVE PRESTRESSED STRANDS. SERIOUS HAZARDS! DAMAGE CAN RESULT FROM A STRAND BEING CUT. GPR SCANNING OF PRECAST CONCRETE AND CMU WALLS IS REQUIRED PRIOR TO CUTTING HOLES IN WALLS. INSTALLING POST-INSTALLED ANCHORS, OR FABRICATING STEEL. NO REINFORCING SHALL BE CUT. IF REINFORCING IS OBSERVED IN THE LOCATION OF THE PROPOSED HOLE OR ANCHOR, IT WILL NEED TO BE RELOCATED.
- CODED NOTES:**
- FIBERGLASS SUPPORT TO EXISTING PRECAST CONCRETE PANEL. COORDINATE LOCATION AND ELEVATION WITH ELECTRICAL DRAWINGS. REFER TO SECTION CUT ON PLAN.
 - WALL MOUNTED ELECTRICAL PULL BOX TO EXISTING PRECAST CONCRETE PANEL. COORDINATE LOCATION AND ELEVATION WITH ELECTRICAL DRAWINGS. FASTENERS NOT TO PROJECT MORE THAN 3/4" INTO PRECAST CONCRETE.
 - 4" THICK CONCRETE HOUSEKEEPING PAD, REFER TO SECTION CUT ON PLAN.
 - PENETRATION IN EXISTING PRECAST PANEL. COORDINATE SIZE AND LOCATION WITH ELECTRICAL DRAWINGS.
 - PENETRATION IN EXISTING 8" CMU WALL. COORDINATE SIZE AND LOCATION WITH ELECTRICAL DRAWINGS.
 - ELECTRICAL CONDUIT, REFER TO ELECTRICAL DRAWINGS.

1 SECOND FLOOR FRAMING PLAN
1/8" = 1'-0"

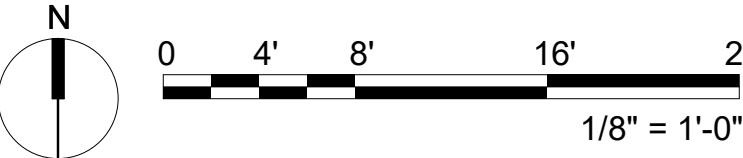

		CONSULTANT	ARCHITECT/ENGINEER OF RECORD  bove Group ENGINEERING DESIGN CONSULTING www.abovegroupinc.com COA/CA Lic. No. 31120 305 East Dr., Suite H, Melbourne, Florida 32904 PH: 321.345.9026		STAMP 	Office of Construction and Facilities Management		Drawing Title SECOND FLOOR FRAMING PLAN		Phase 100% CONSTRUCTION DOCUMENTS		Project Title INSTALL ALTERNATE CONNECTIONS FOR STEAM AND CHILLED WATER		Project Number 516-22-602	
Building Number															
Drawing Number															
SS102															
Revisions		Date													

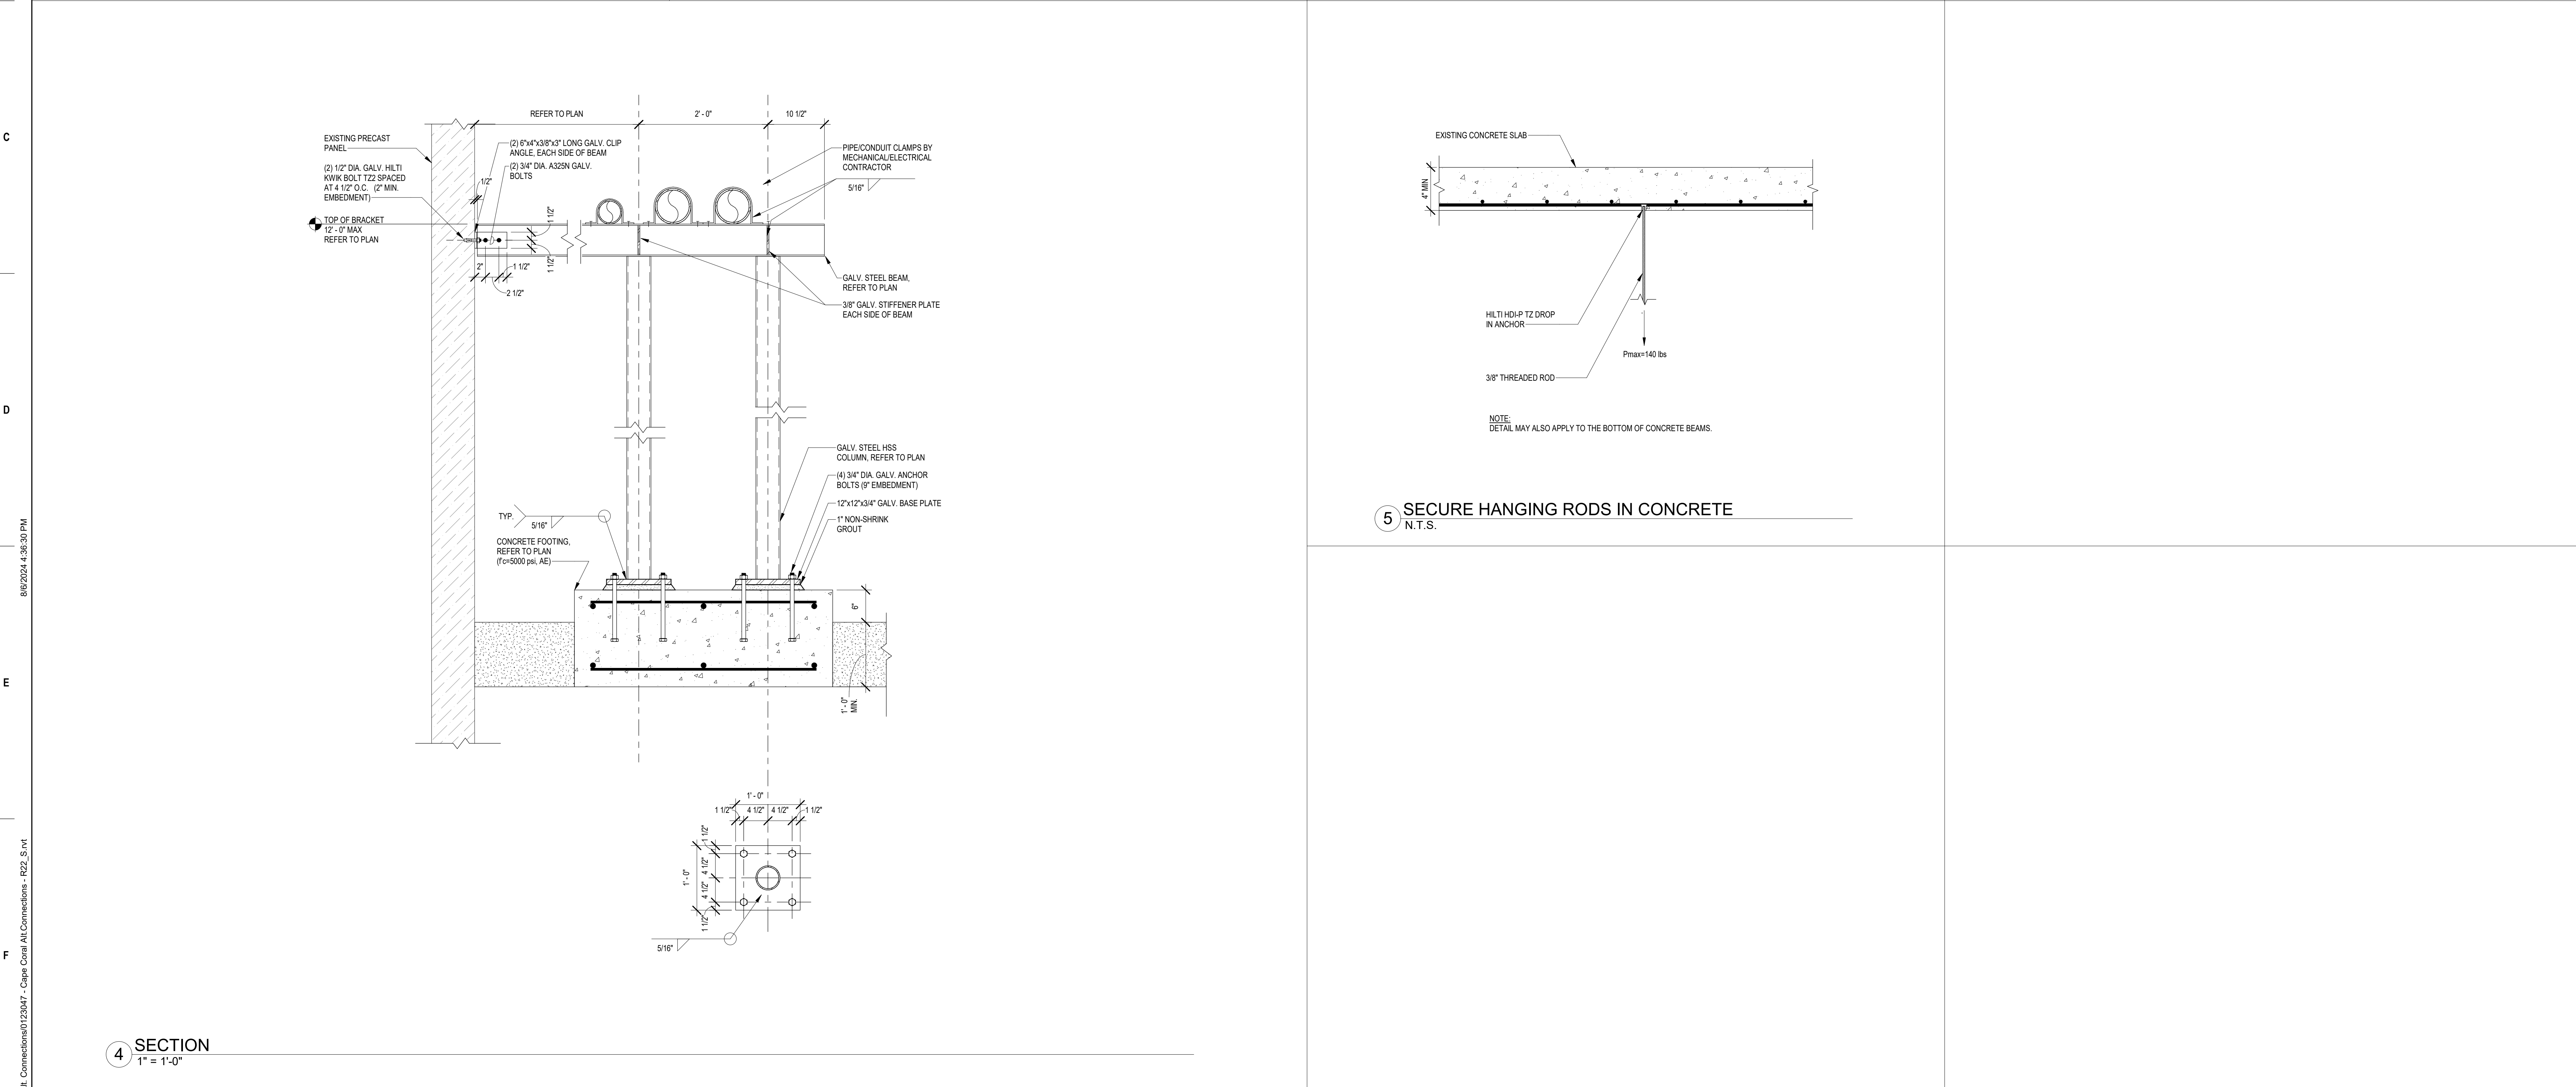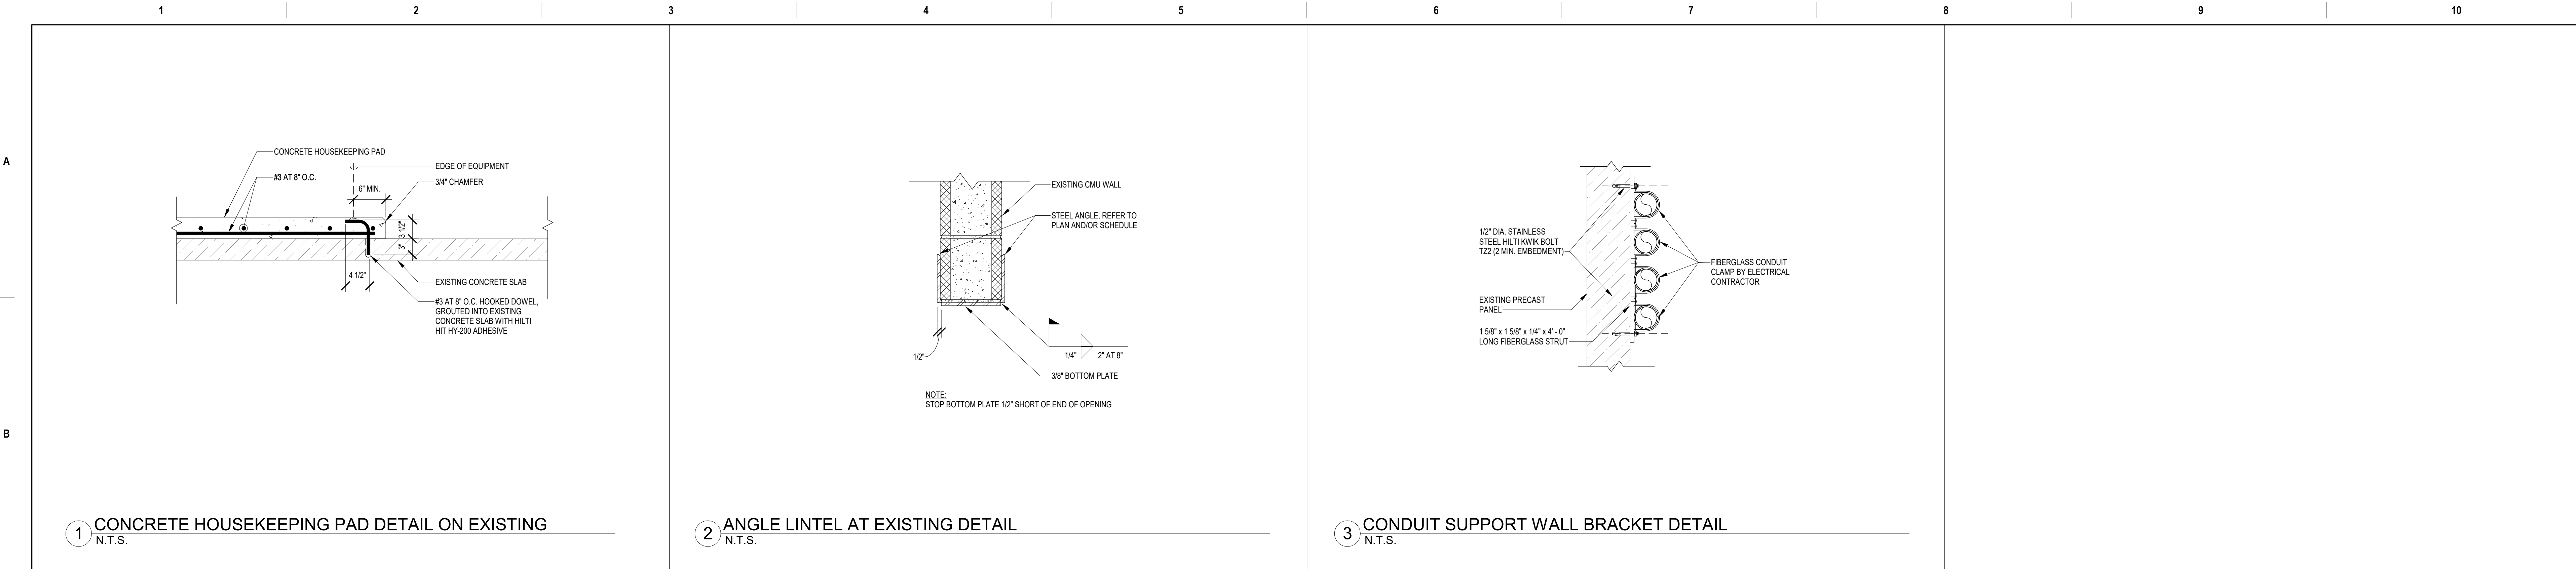


Autodesk Docs/0123047 - VA Cape Coral	</
--	--	----

VA FORM 08-6231

305 East Dr., Suite H,
Melbourne, Florida 32904
PH: 321.345.9026

VA U.S. Department of
Veterans Affairs

M-001

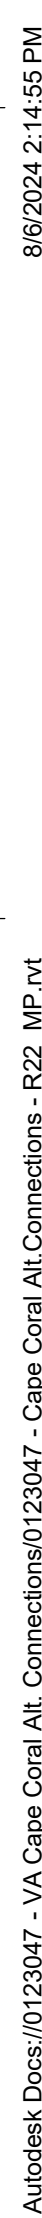


5 ALLOTTED LOCATION FOR FUTURE TEMPORARY RENTAL CHILLER, SEE MP101.


1 $1'' = 30'-0''$

		CONSULTANT		ARCHITECT/ENGINEER OF RECORD  www.abovegroupinc.com COA/CA Lic. No. 31120		STAMP 		Office of Construction and Facilities Management VA U.S. Department of Veterans Affairs		Drawing Title MECHANICAL SITE PLAN Approved:		Phase 100% CONSTRUCTION DOCUMENTS		Project Title INSTALL ALTERNATE CONNECTIONS FOR STEAM AND CHILLED WATER		Project Number 516-22-602 Building Number		Drawing Number MS100	
Revisions		Date								Location CAPE CORAL VA		Issue Date 08/07/2024		Checked RHA		Drawn WRH			

- CODED NOTES:
- ① DEMOLISH PIPING AND PREPARE, AS REQUIRED, TO INSTALL PIPING CONNECTIONS SHOWN ON NEW WORK DRAWINGS.
 - ② DEMOLISH EXISTING WALL STRUCTURE AND PREPARE FOR SLEEVES AND SLEEVE SEALS AS SHOWN ON NEW WORK DRAWINGS. REFER TO SPECIFICATIONS AND DETAILS.

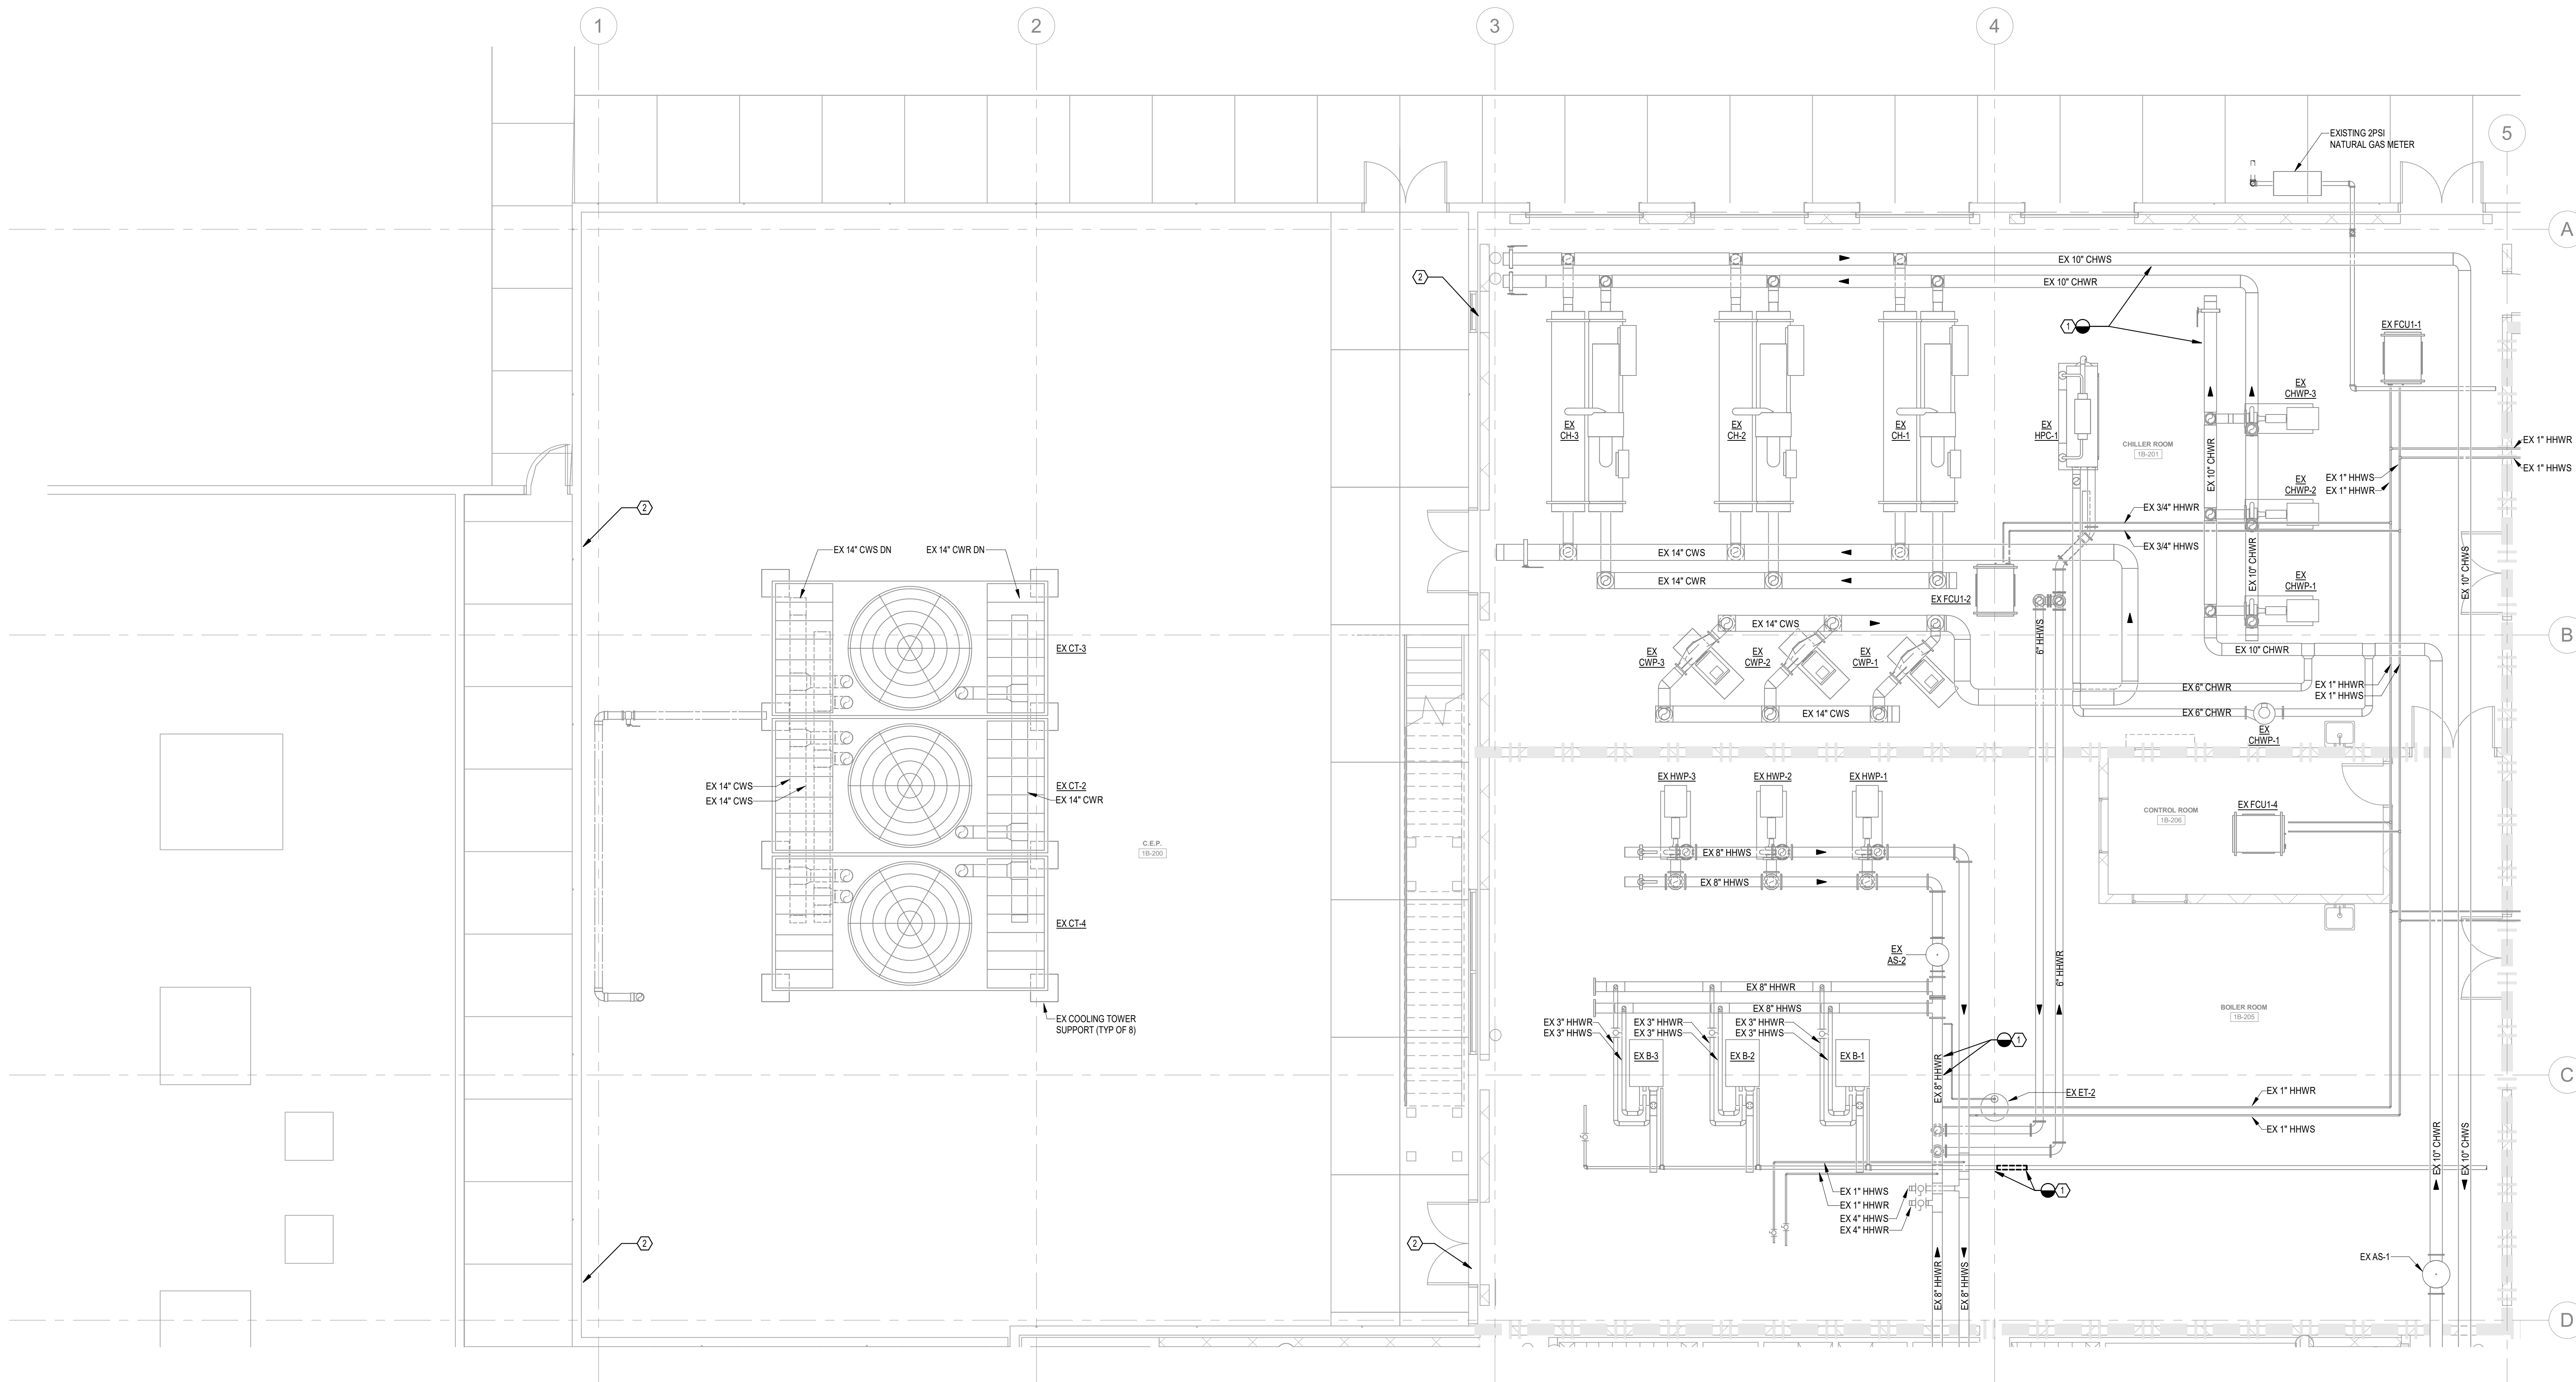

① PARTIAL FIRST FLOOR PLAN - MECHANICAL - DEMOLITION
3/16" = 1'-0"

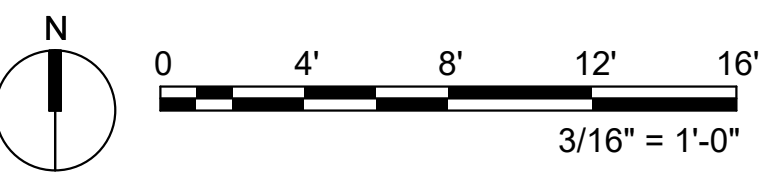

--	--	

AutoCAD Doc: 10123047 - VA Cape Coral Alt. Connections 10123047 - Cape Coral Alt. Connections - R02 - MP.rvt
8/8/2024 2:14:43 PM
VA FORM 08 - 6231

SIGNAGE INSTRUCTIONS

SIGNAGE GENERAL FORMAT:

CONNECTIONS FOR TEMPORARY (INSERT SYSTEM NAME)
CONTRACTOR TO PROVIDE FINAL CONNECTIONS AND VERIFY ALL
POWER AND PERFORMANCE REQUIREMENTS PRIOR TO
INSTALLATION AND CONNECTION OF TEMPORARY EQUIPMENT.

GENERAL SIGNAGE NOTES:


1. SIGNS SHALL BE MINIMUM 16 INCH SQUARE.
2. SIGNS SHALL BE RATED FOR OUTDOOR CONDITIONS.
3. SIGNS TO BE ASTM B209 ALUMINUM SHEET, BLACK ENGRAVED LETTERING ON WHITE BOND, BAKED ENAMEL COATED FINISH.

GENERAL NOTES


1. SEE M-7 SERIES SHEETS FOR PIPING DIAGRAMS FOR COMPLETE REQUIREMENTS OF ALL VALVES AND ACCESSORIES AS PART OF THIS SCOPE OF WORK.


CODED NOTES:

- | | | | |
|---|---|---|--|
| ① | VALVE AND CAP CONNECTIONS FOR TEMPORARY EQUIPMENT AT APPROXIMATELY 4 FT ABOVE GRADE | ⑦ | HOT TAP PIPING INTO EXISTING SYSTEM IT IS TO BE ASSURED THAT NO SHUTDOWNS ARE ALLOWABLE FOR CHILLED WATER SYSTEM IE. VERIFY WITH FACILITY ENGINEERING CHER PRIOR TO START OF WORK. |
| ② | MAINTAIN APPROPRIATE CLEARANCE AROUND EXISTING ELECTRICAL GEAR. | ⑧ | POINT OF CONNECTION FOR HEATING HOT WATER SYSTEM. COORDINATE SHUTDOWN WITH FACILITY CHER PRIOR TO START OF WORK. SHUTDOWN LASTING LONGER THAN 4 HOURS IS NOT ALLOWED. |
| ③ | IN THE EVENT OF A COOLING TOWER FAILURE, FAULT, OR PROLONGED MAINTENANCE PERIOD, CONNECT TEMPORARY AIR-COOLED CHILLER TO NEW CHWSR PIPING CONNECTIONS SHOWN. | ⑨ | POINT OF CONNECTION FOR NATURAL GAS. COORDINATE SHUTDOWN WITH FACILITY CHER PRIOR TO START OF WORK. PROVIDE UPSURGE AND DOWNSURGE ISOLATION VALVES AT POINT OF CONNECTION. |
| ④ | IN THE EVENT OF A WATER-COOLED CHILLER FAILURE, FAULT, OR PROLONGED MAINTENANCE PERIOD, CONNECT TEMPORARY AIR-COOLED CHILLER TO NEW CHWSR PIPING CONNECTIONS SHOWN. | ⑩ | PROVIDE EQUIPMENT TAG SIGN NEAR VALVE CONNECTIONS WITH CAPACITY REQUIREMENTS FOR TEMPORARY CHILLER AND PUMP AS INDICATED ON M-102. |
| ⑤ | IN THE EVENT OF A BOILER FAILURE, FAULT, OR PROLONGED MAINTENANCE PERIOD, CONNECT TEMPORARY BOILER TO NEW HWHSR PIPING CONNECTIONS SHOWN. | ⑪ | PROVIDE EQUIPMENT TAG SIGN NEAR VALVE CONNECTIONS WITH CAPACITY REQUIREMENTS FOR TEMPORARY HEATING HOT WATER BOILER SYSTEM AS INDICATED ON M-102. |
| ⑥ | PROVIDE ULTRASONIC CLAMP-ON FLOWMETER AT LOCATION SHOWN AS PART OF BTU ENERGY METER SYSTEM. INCLUDE A REMOTE MOUNTED FLOW COMPUTER FOR EACH FACILITY LOCATION AND A PAIR OF TEMPERATURE-RESISTANT FLOWMETERS. LOCATE FLOW COMPUTER AT 5'± ABOVE FINISHED FLOOR ON AN ADJACENT WALL OR COLUMN NEAR FLOW METER. REFER TO FLOW METER DETAIL FOR MINIMUM REQUIREMENTS. INSTALL WITH STRAIGHT DIAMETER INLET AND OUTLET PER MANUFACTURER'S INSTRUCTIONS. | ⑫ | TEMPORARY DDC PANEL (CHW). PROVIDE 120-140 POWER. |
| | | ⑬ | TEMPORARY DDC PANEL (HHW). PROVIDE 120-140 POWER. |

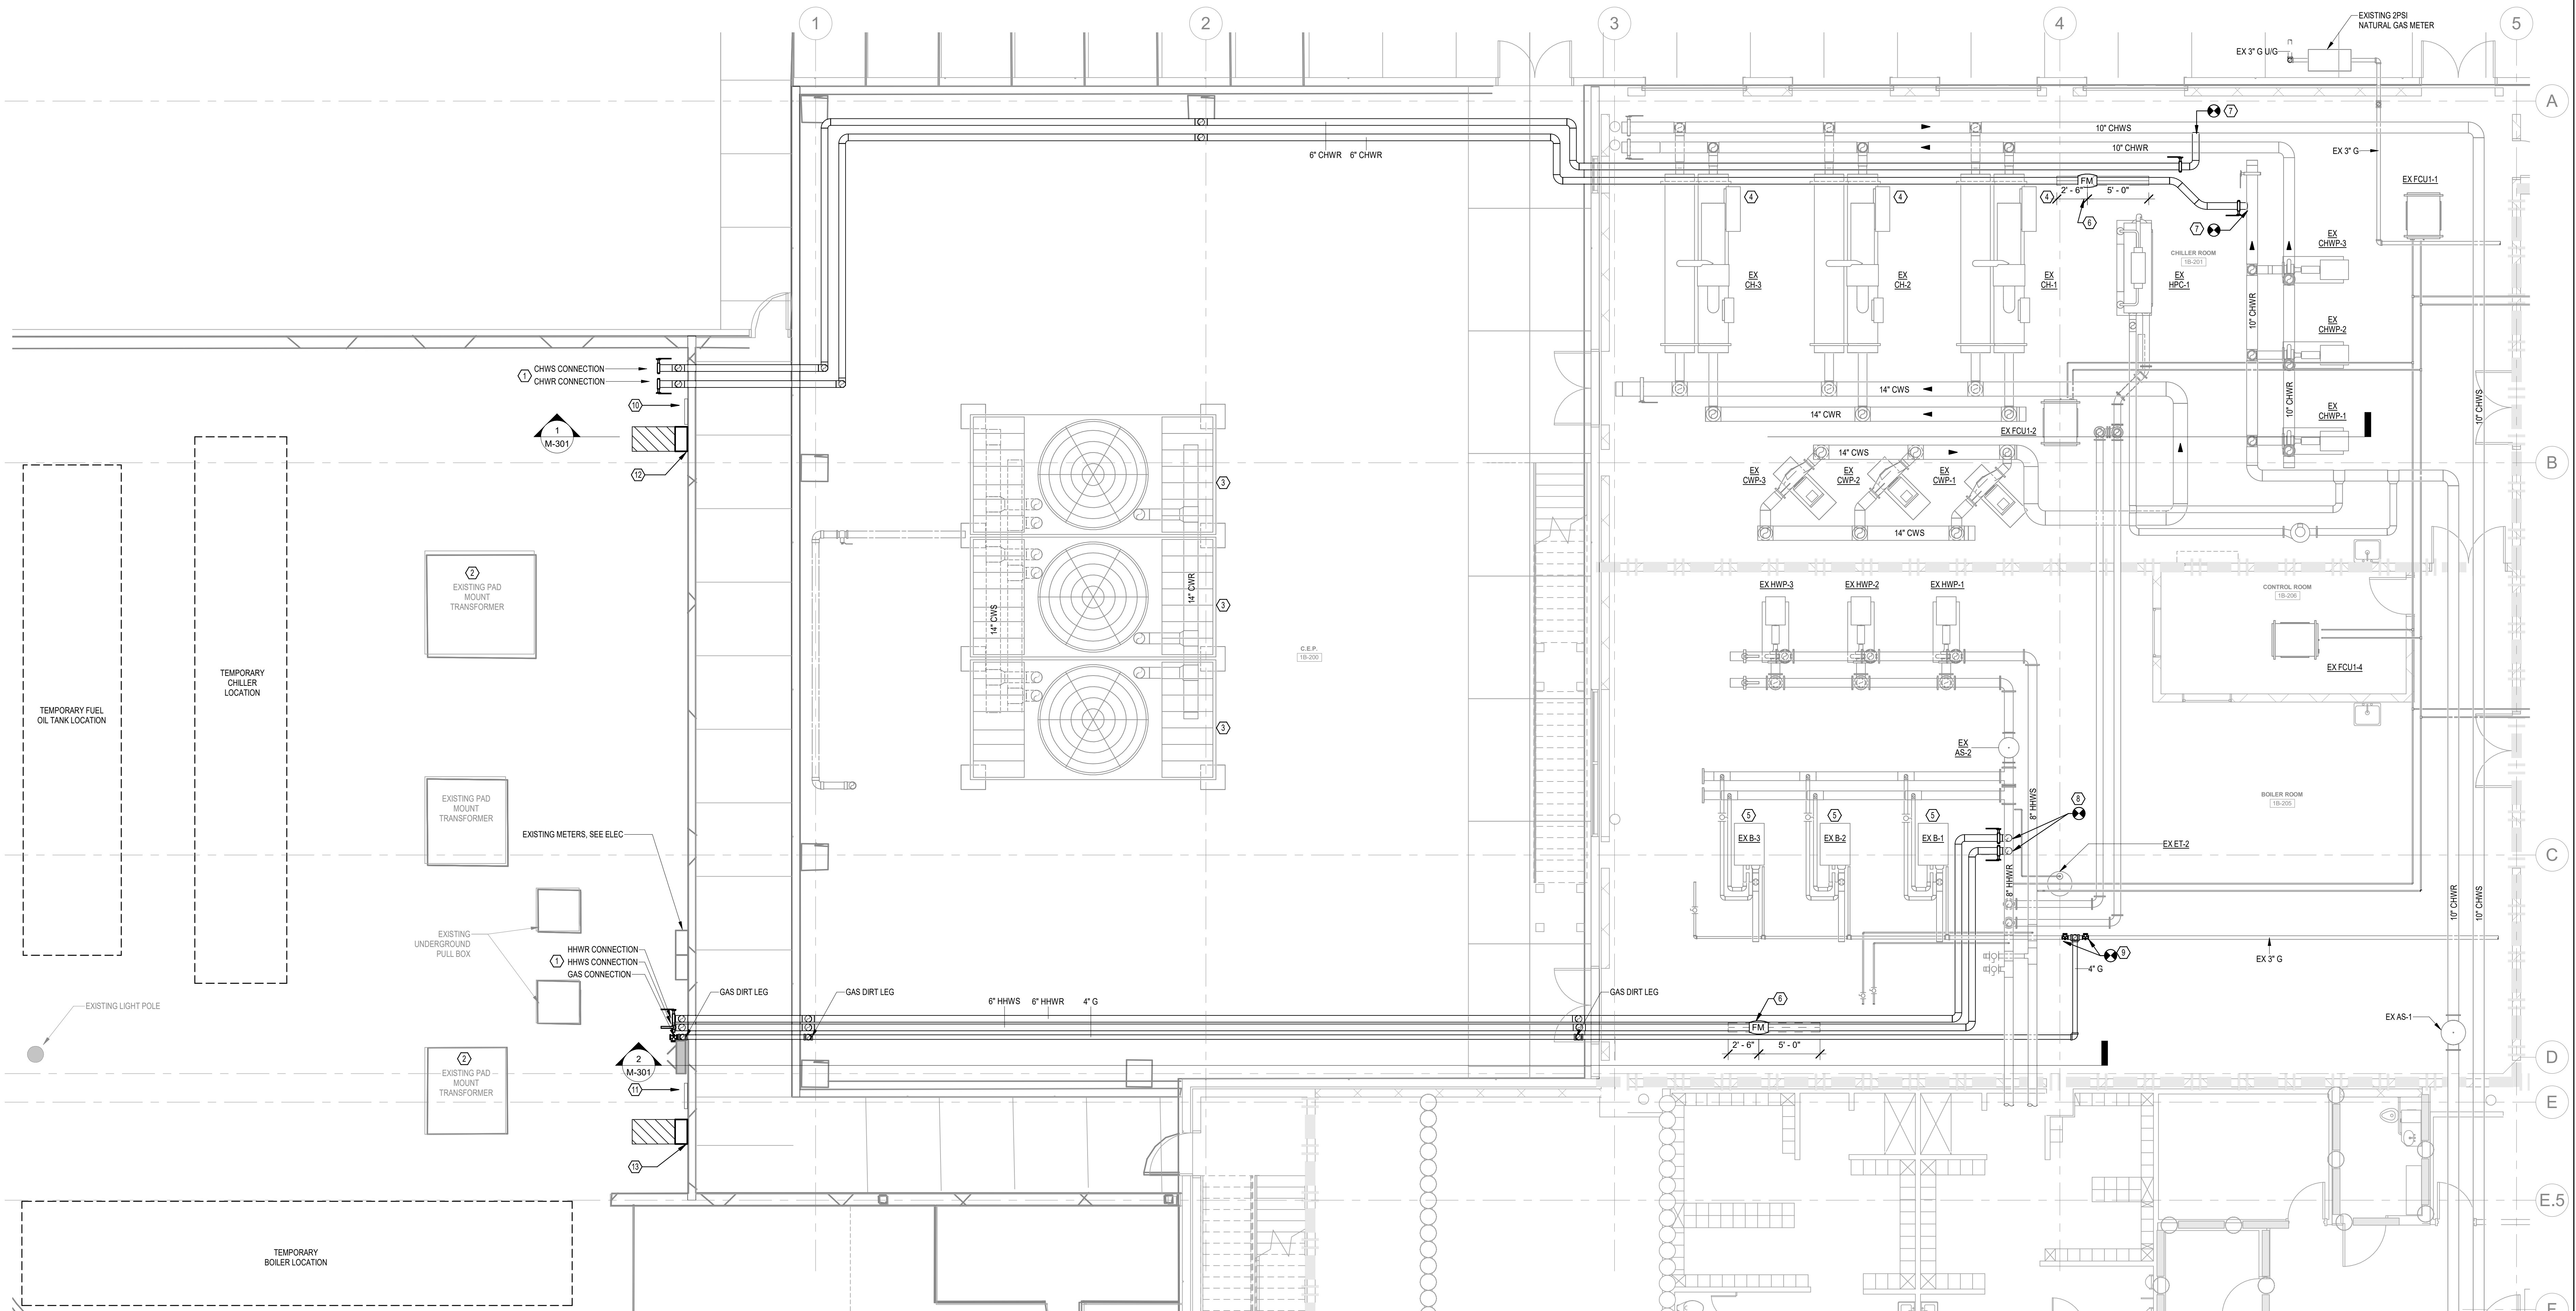

1 FIRST FLOOR PLAN - MECHANICAL - NEW WORK
3/16" = 1'-0"

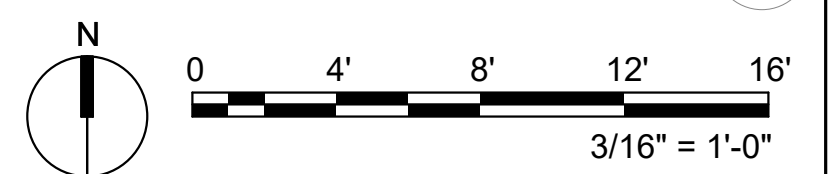[illegible]

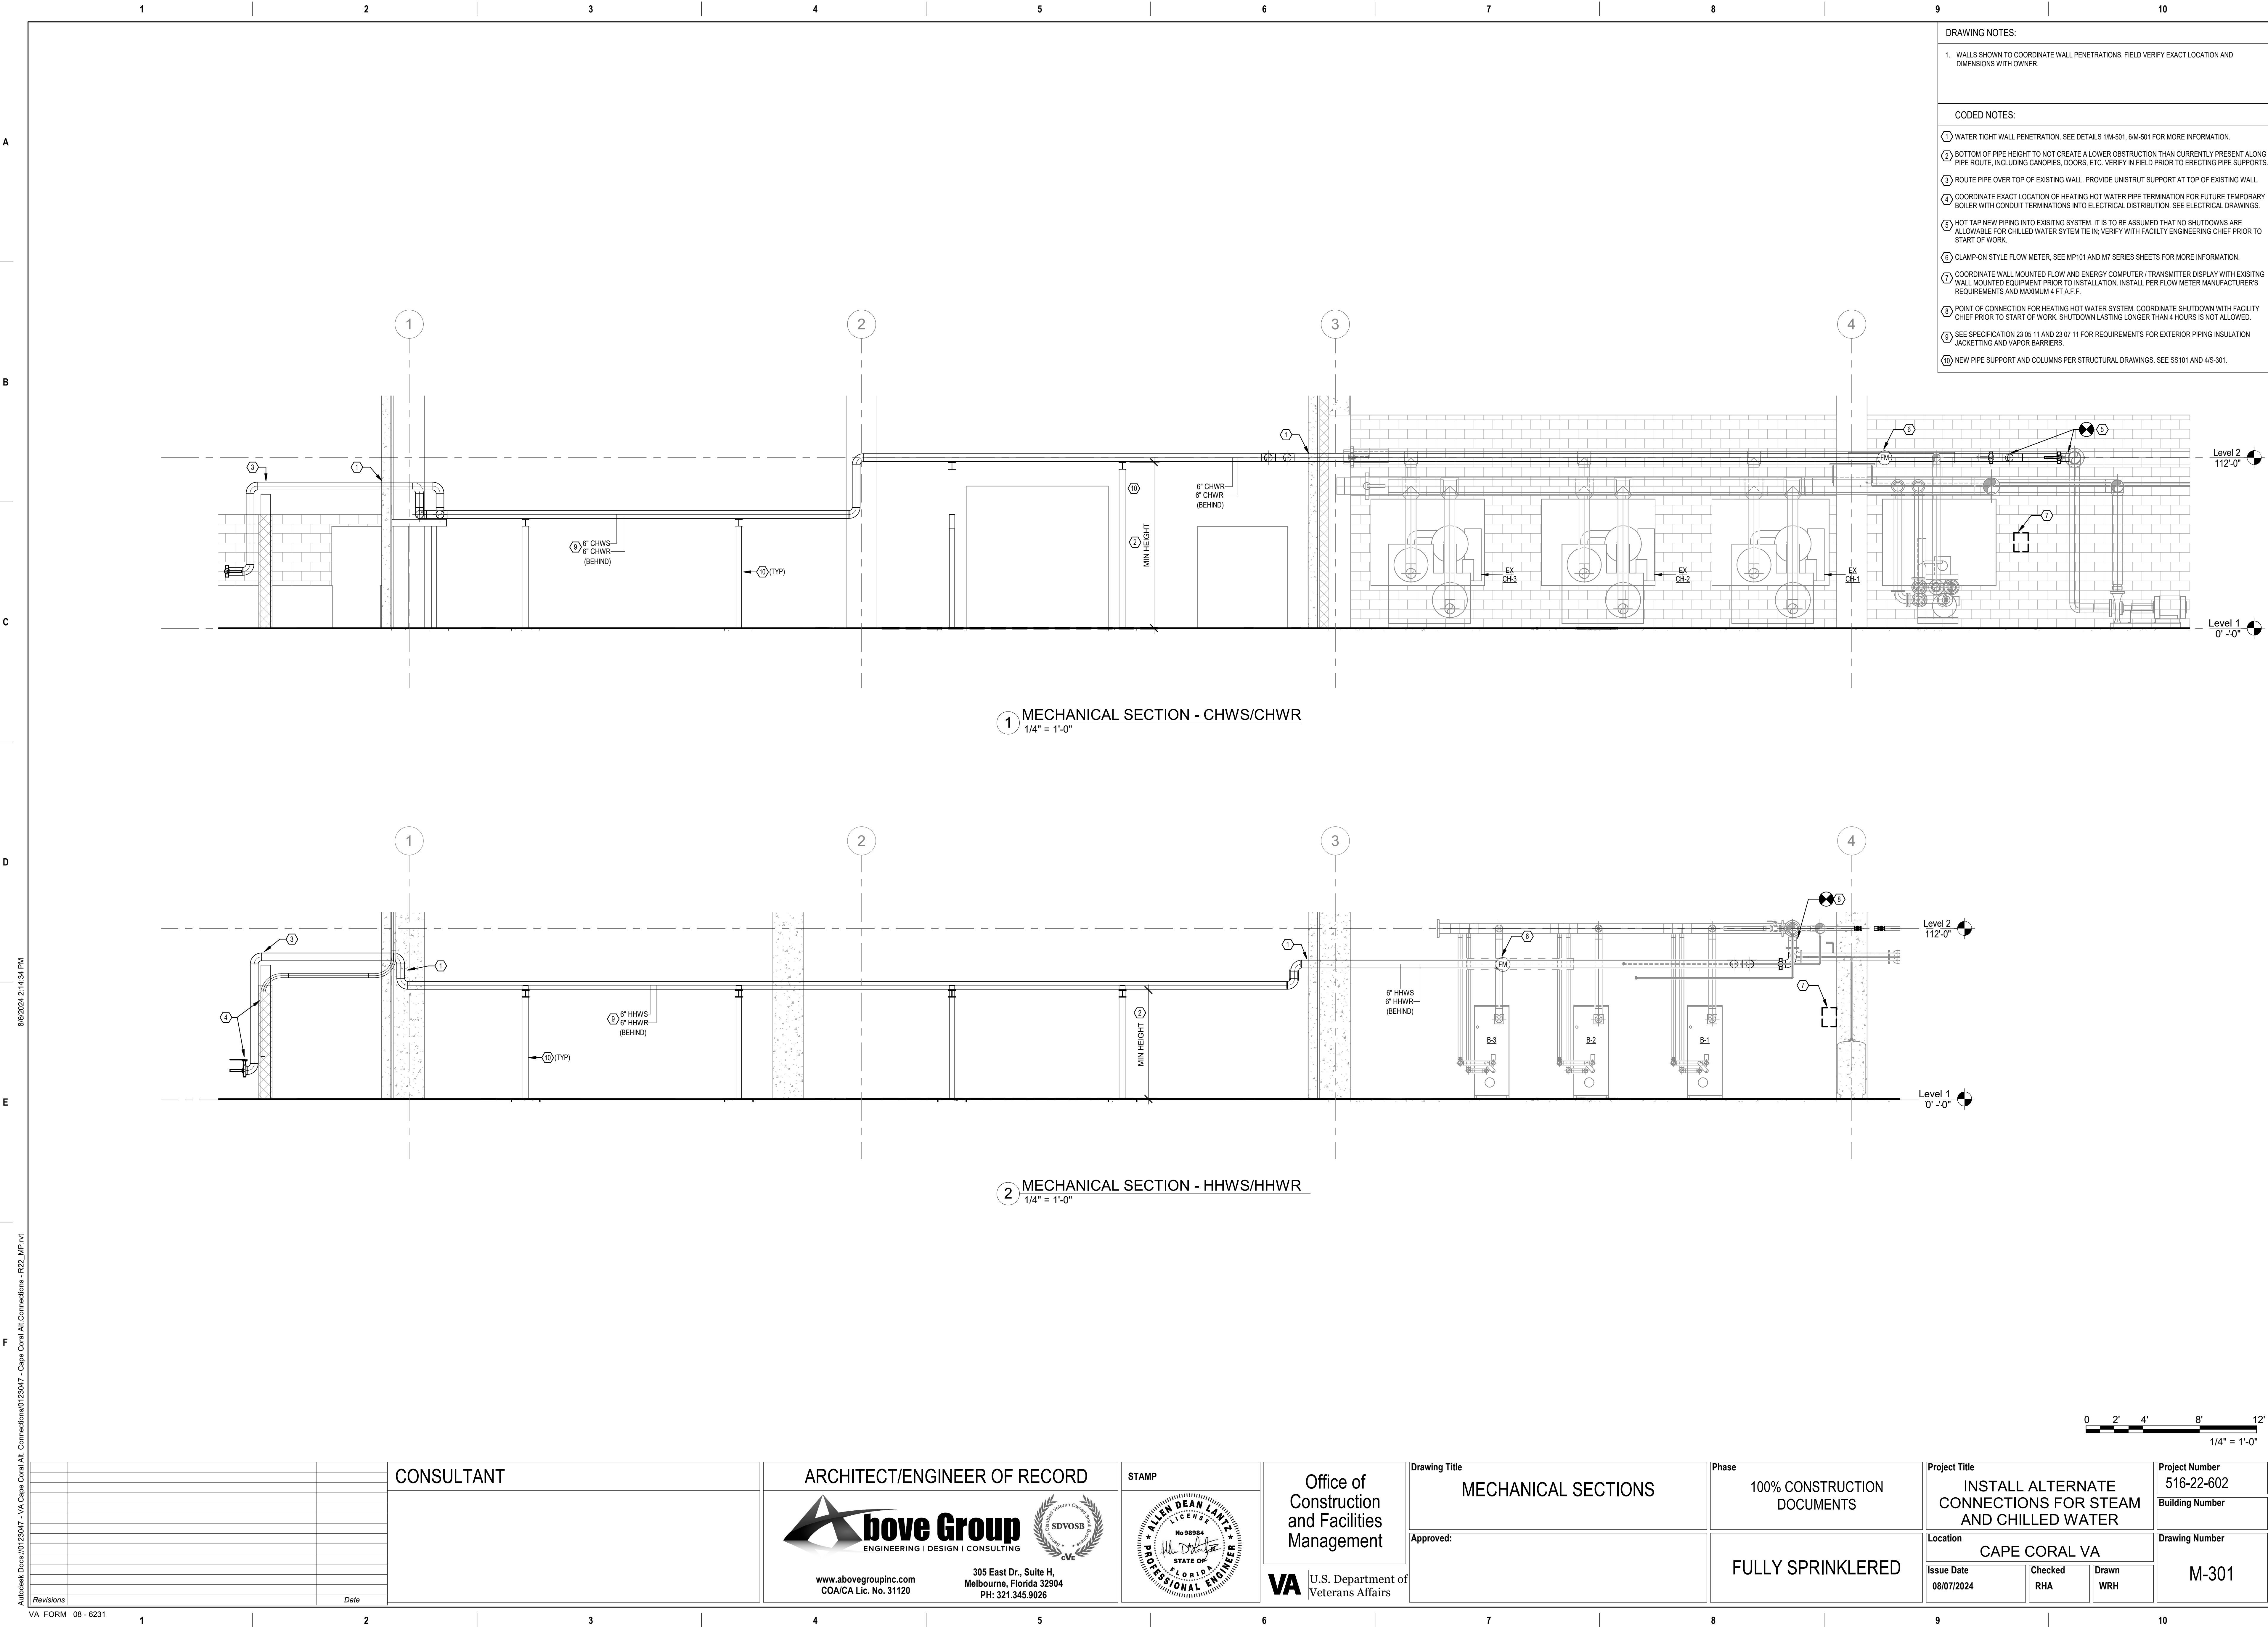

- DRAWING NOTES:
1. WALLS SHOWN TO COORDINATE WALL PENETRATIONS. FIELD VERIFY EXACT LOCATION AND DIMENSIONS WITH OWNER.
- CODED NOTES:
- ① WATER TIGHT WALL PENETRATION. SEE DETAILS 1M-501, 6M-501 FOR MORE INFORMATION.
- ② BOTTOM OF PIPE HEIGHT TO NOT CREATE A LOWER OBSTRUCTION THAN CURRENTLY PRESENT ALONG PIPE ROUTE, INCLUDING CANOPIES, DOORS, ETC. VERIFY IN FIELD PRIOR TO ERECTING PIPE SUPPORTS.
- ③ ROUTE PIPE OVER TOP OF EXISTING WALL. PROVIDE UNISTRUT SUPPORT AT TOP OF EXISTING WALL.
- ④ COORDINATE EXACT LOCATION OF HEATING HOT WATER PIPE TERMINATION FOR FUTURE TEMPORARY BOILER WITH CONDUIT TERMINATIONS INTO ELECTRICAL DISTRIBUTION. SEE ELECTRICAL DRAWINGS.
- ⑤ HOT TAP NEW PIPING INTO EXISTING SYSTEM. IT IS TO BE ASSUMED THAT NO SHUTDOWNS ARE ALLOWABLE FOR CHILLED WATER SYSTEM TIE IN. VERIFY WITH FACILITY ENGINEERING CHIEF PRIOR TO START OF WORK.
- ⑥ CLAMP-ON STYLE FLOW METER. SEE MP101 AND M7 SERIES SHEETS FOR MORE INFORMATION.
- ⑦ COORDINATE WALL MOUNTED FLOW AND ENERGY COMPUTER / TRANSMITTER DISPLAY WITH EXISTING WALL MOUNTED EQUIPMENT PRIOR TO INSTALLATION. INSTALL PER FLOW METER MANUFACTURER'S REQUIREMENTS AND MAXIMUM 4 FT A.F.F.
- ⑧ POINT OF CONNECTION FOR HEATING HOT WATER SYSTEM. COORDINATE SHUTDOWN WITH FACILITY CHIEF PRIOR TO START OF WORK. SHUTDOWN LASTING LONGER THAN 4 HOURS IS NOT ALLOWED.
- ⑨ SEE SPECIFICATION 23 05 11 AND 23 07 11 FOR REQUIREMENTS FOR EXTERIOR PIPING INSULATION JACKETING AND VAPOR BARRIERS.
- ⑩ NEW PIPE SUPPORT AND COLUMNS PER STRUCTURAL DRAWINGS. SEE SS101 AND 4IS-301.

A

B

C

D

E

F

A


B

C


D

E

F

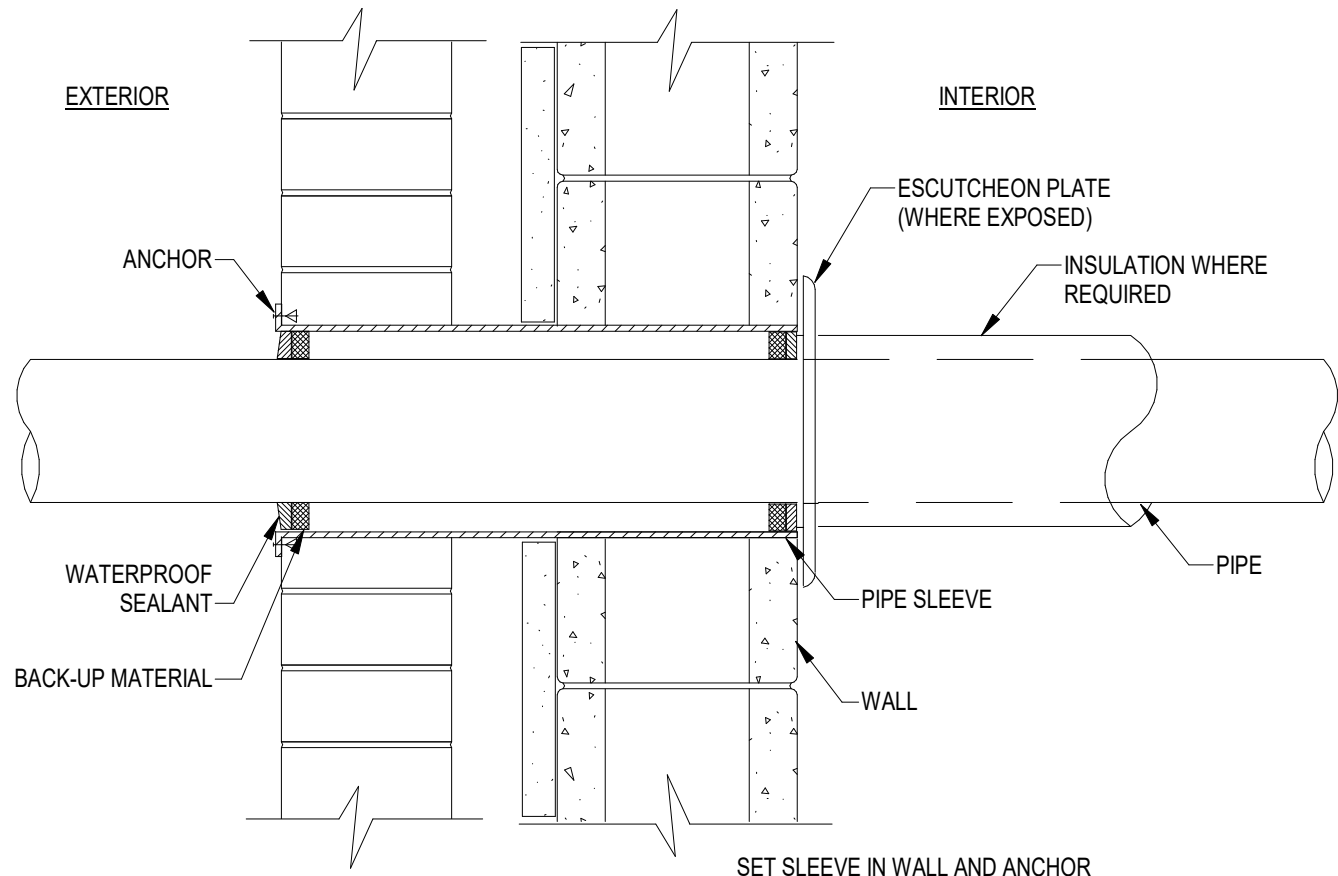


1 PIPING EXTERIOR WALL PENETRATION DETAIL
N.T.S.

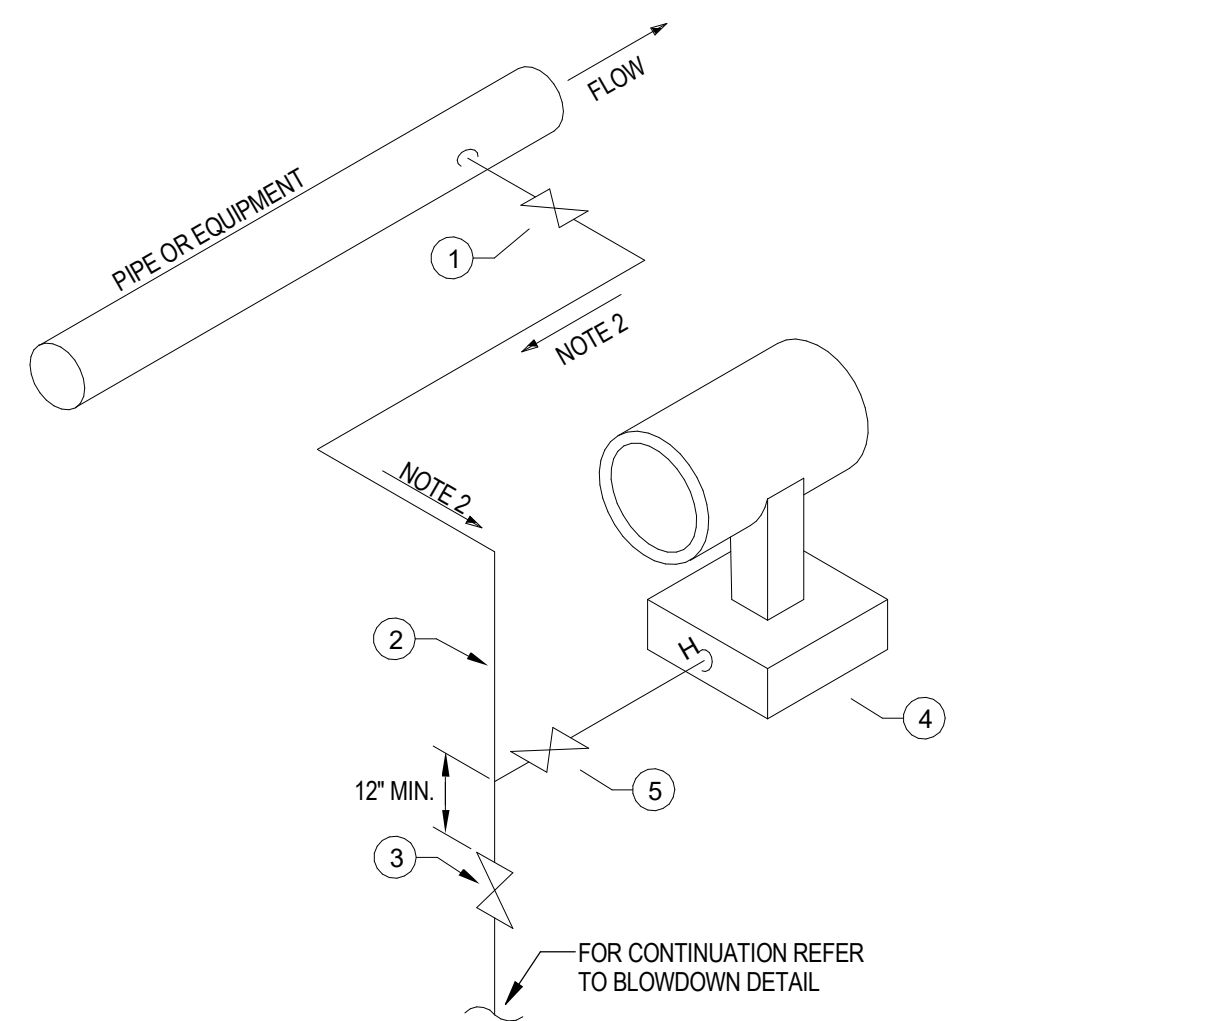


- NOTES:
- DO NOT INSTALL BLOWDOWN VALVES OR TUBING ON FLAMMABLE OR TOXIC LIQUIDS OR GAS.
 - SLOPE: 1/2" PER FOOT MINIMUM ONE INCH PER FOOT PREFERRED.
 - OPTIONAL VALVE TO BE INSTALLED IF ACCESS TO ITEM 1 VALVE.
 - REQUIRES MORE THAN A SIX FOOT STEP LADDER.
- | ITEM DESCRIPTION |
|----------------------------|
| 1 ISOLATION VALVE |
| 2 PIPE OR TUBE |
| 3 BLOWDOWN VALVE |
| 4 TRANSMITTER OR SWITCH |
| 5 OPTIONAL ISOLATION VALVE |

2 PRESSURE TRANSMITTER
N.T.S.

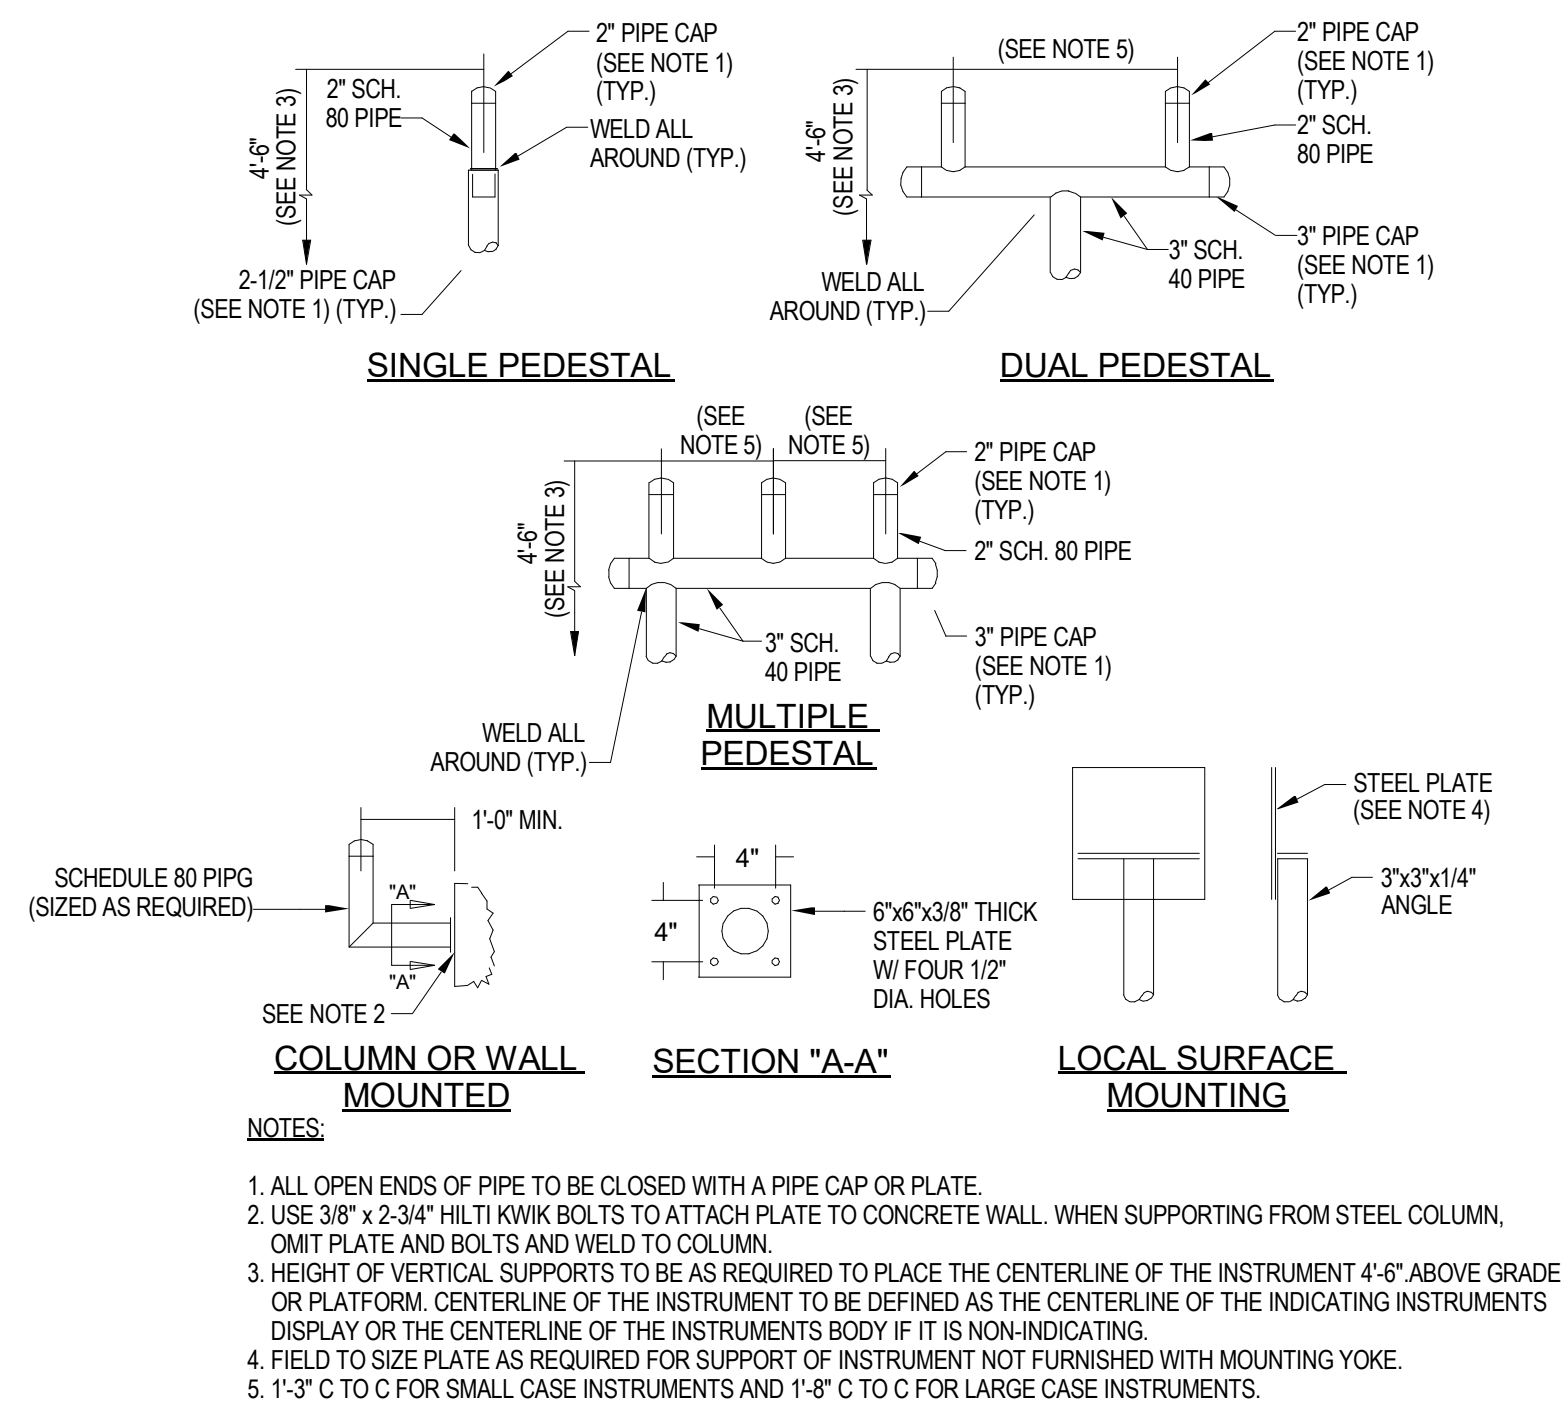


3 INSTRUMENTATION INSTALLATION DETAIL
N.T.S.

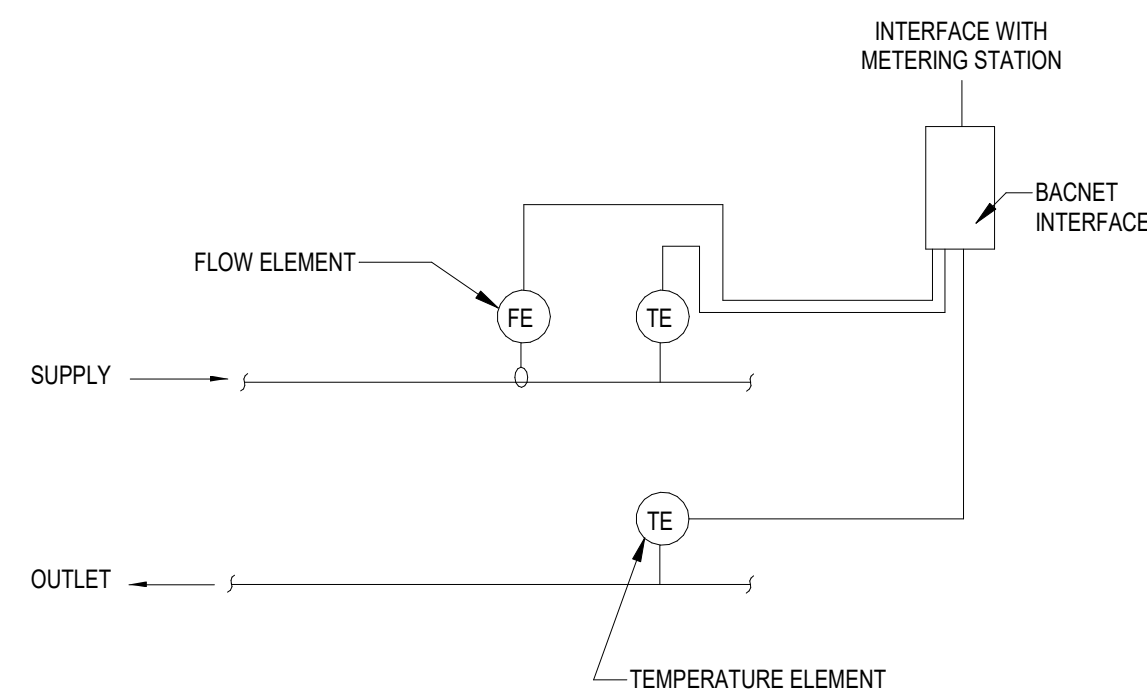


- NOTES:
- UPSTREAM AND DOWNSTREAM CONDITIONS SHALL BE PER FLOW METER DETAIL OR FLOW METER MANUFACTURER, WHICHEVER IS MORE STRINGENT.
 - TEMPERATURE ELEMENTS SHALL BE A MATCHED PAIR. REFER TO P&ID FOR LOCATION AND ADDITIONAL REQUIREMENTS FOR CONTROLS AND MONITORING.

4 WATER FLOW MEASURING STATION (WITH BTU METER)
N.T.S.

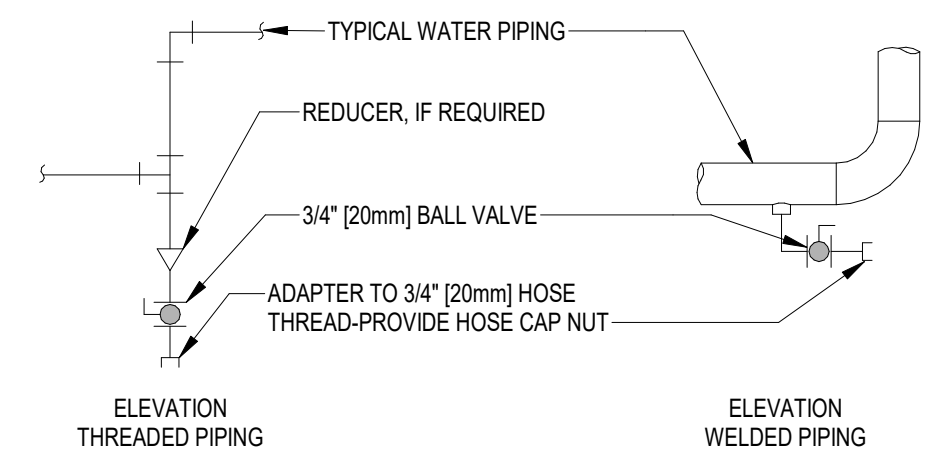


- NOTES:
- DRAIN ALL LOW POINTS AS INDICATED ABOVE.
 - WHERE SCALE POCKETS ARE SHOWN ON PIPE RISER DIAGRAMS AND/OR PLANS LOCATE DRAIN AT BOTTOM OF SCALE POCKET.

TYPICAL CHILLED AND HOT WATER PIPING DRAIN VALVE CONNECTIONS

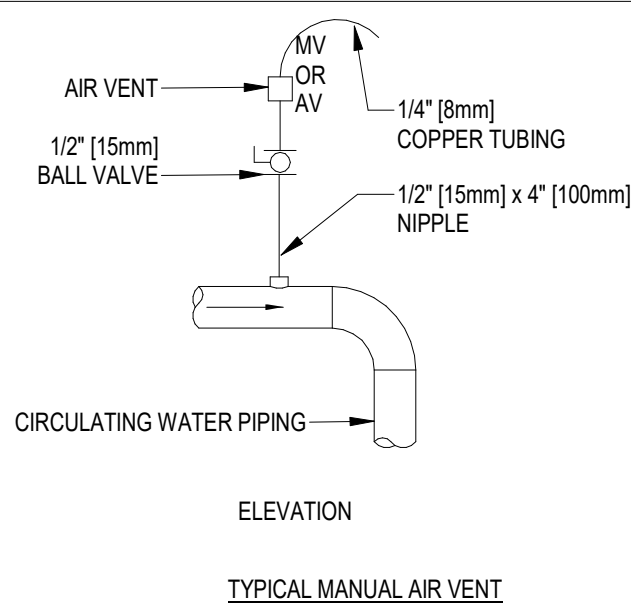


5 DRAIN VALVE AND AIR VENT CONNECTIONS
N.T.S.

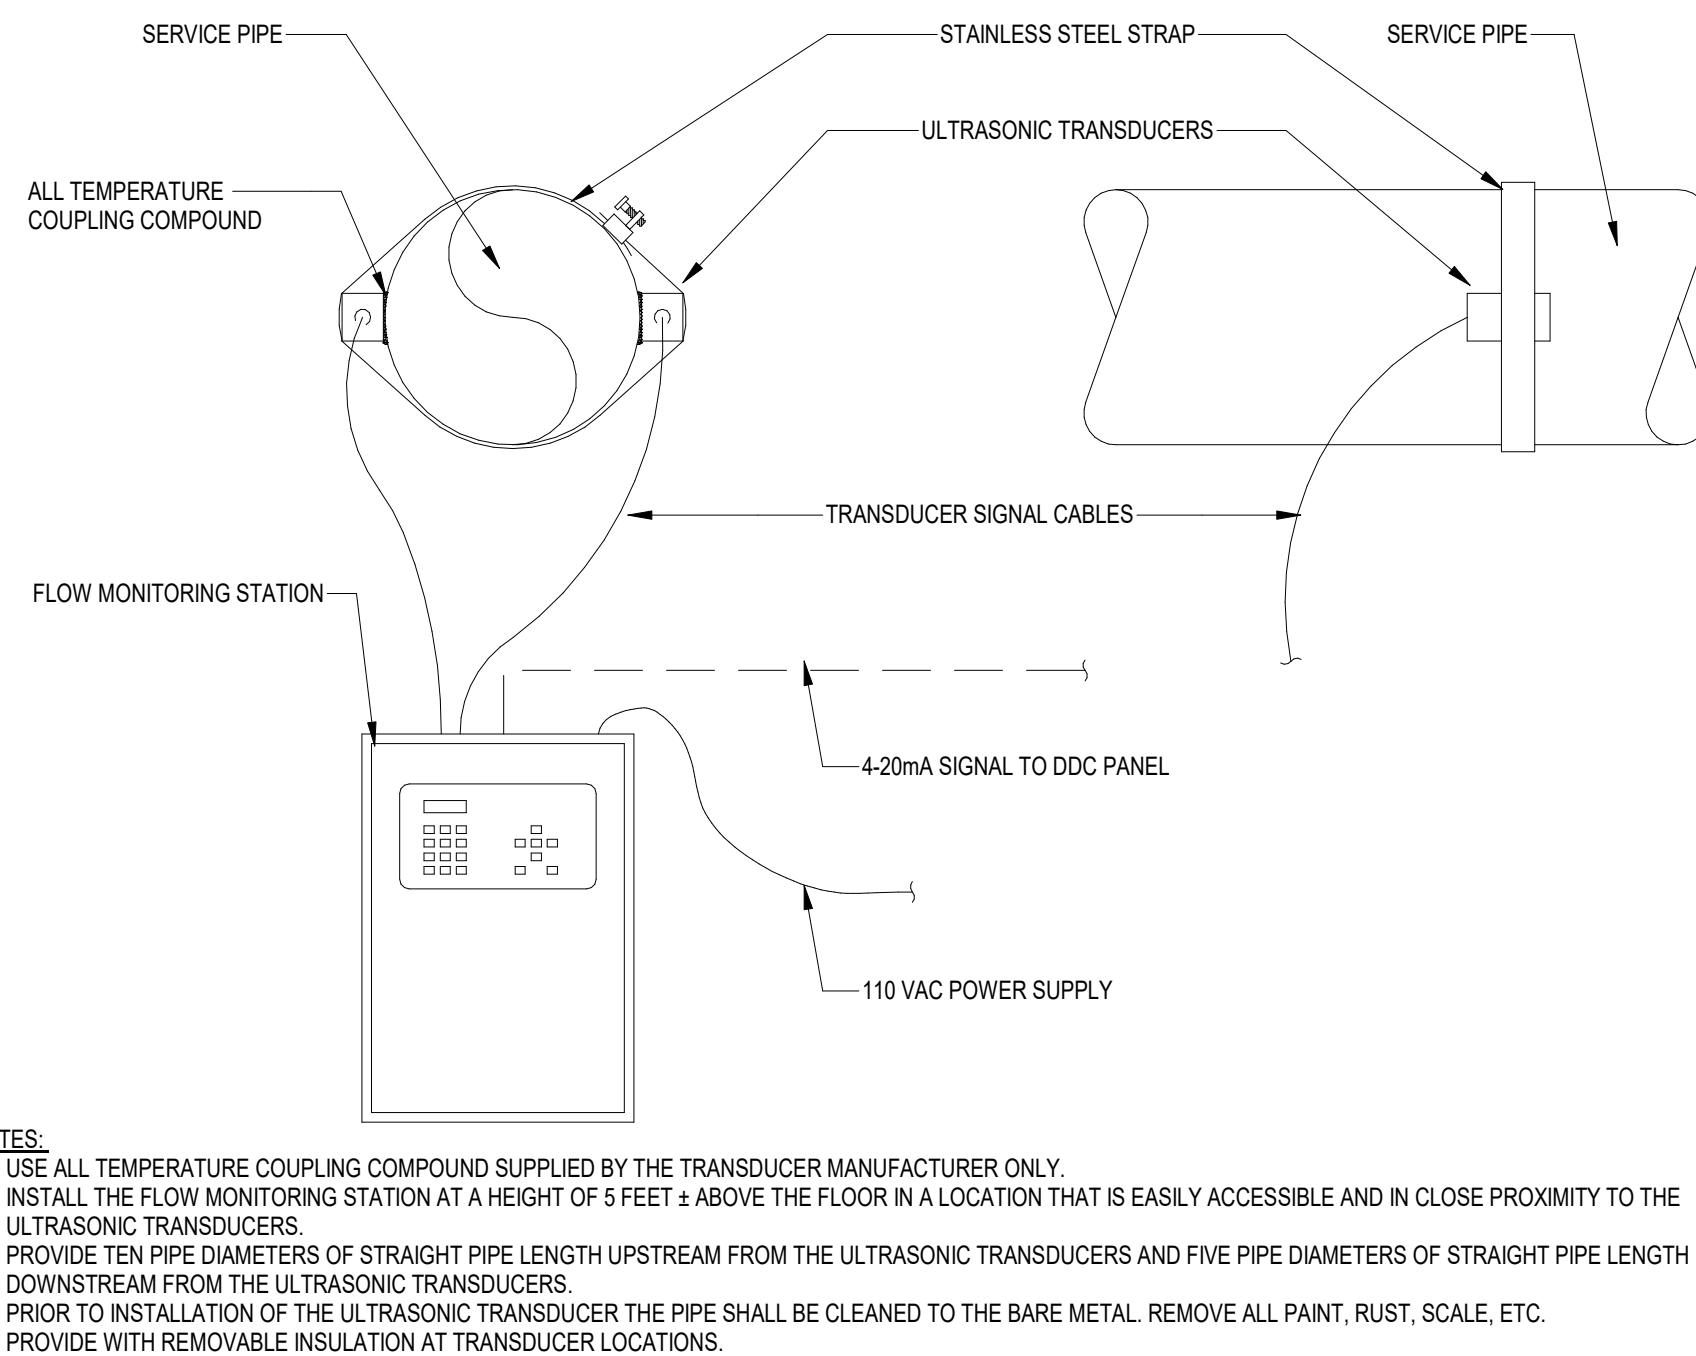

- NOTES:
- USE ALL TEMPERATURE COUPLING COMPOUND SUPPLIED BY THE TRANSDUCER MANUFACTURER ONLY.
 - INSTALL THE FLOW MONITORING STATION AT A HEIGHT OF 5 FEET ± ABOVE THE FLOOR IN A LOCATION THAT IS EASILY ACCESSIBLE AND IN CLOSE PROXIMITY TO THE ULTRASONIC TRANSDUCERS.
 - PROVIDE TEN PIPE DIAMETERS OF STRAIGHT PIPE LENGTH UPSTREAM FROM THE ULTRASONIC TRANSDUCERS AND FIVE PIPE DIAMETERS OF STRAIGHT PIPE LENGTH DOWNSTREAM FROM THE ULTRASONIC TRANSDUCERS.
 - PRIOR TO INSTALLATION OF THE ULTRASONIC TRANSDUCER THE PIPE SHALL BE CLEANED TO THE BARE METAL. REMOVE ALL PAINT, RUST, SCALE, ETC.
 - PROVIDE WITH REMOVABLE INSULATION AT TRANSDUCER LOCATIONS.

6 FLOW METER DETAIL
N.T.S.

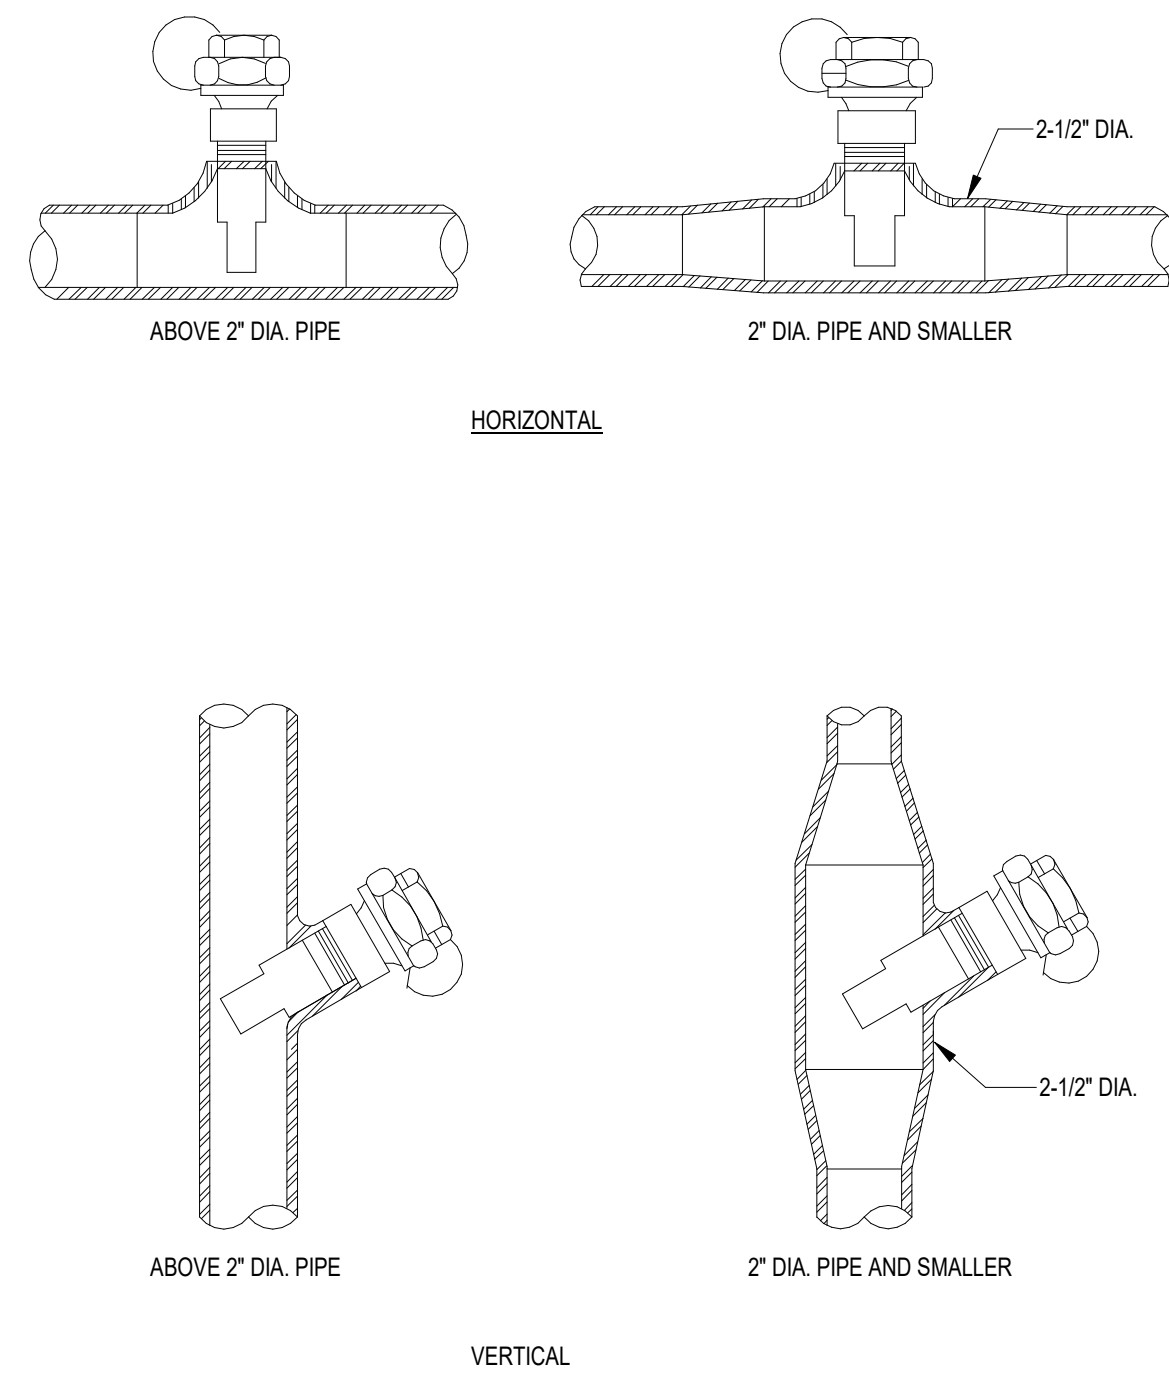

7 INSTALLATION OF THERMOMETER WELLS
N.T.S.

8/6/2024 2:14:35 PM

Autodesk Docs\0123047 - VA Cape Coral AL Connections\0123047 - Cape Coral AL Connections - R22 - MP.rvt

CONSULTANT


ARCHITECT/ENGINEER OF RECORD



www.abovegroupinc.com
COA/ICA Lic. No. 31120

305 East Dr., Suite H,
Melbourne, Florida 32904
PH: 321.345.9026

STAMP

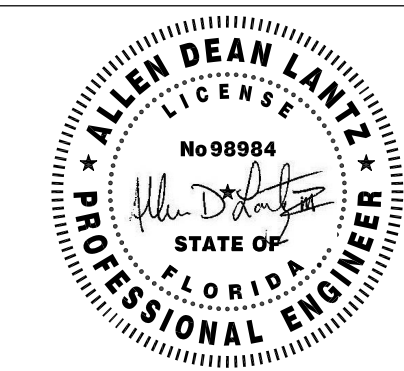

Office of
Construction
and Facilities
Management

VA

U.S. Department of
Veterans Affairs

Drawing Title

MECHANICAL DETAILS

Approved:

Phase

100% CONSTRUCTION
DOCUMENTS

FULLY SPRINKLERED

Project Title

INSTALL ALTERNATE
CONNECTIONS FOR STEAM
AND CHILLED WATER

Location

CAPE CORAL VA

Issue Date
08/07/2024

Checked
RHA

Drawn
WRH

Project Number

516-22-602

Building Number

Drawing Number

M-501

A

B

C

D

E

F

8/6/2024 2:14:37 PM

Autodesk Docs\0123047 - VA Cape Coral Alt. Connections\0123047 - Cape Coral Alt. Connections - R02_MF.rvt

- CODED NOTES:**
- TEMPORARY CHILLED WATER PIPING - PROVIDE AT THE TIME OF EQUIPMENT RENTAL. MINIMUM SIZE REQUIRED FOR DESIGN FLOW CONDITIONS IS 8 INCHES.
 - MATCHED PAIR SUPPLY AND RETURN TEMPERATURE TRANSMITTERS - PROVIDE THERMOWELLS. PROVIDE AI (SUPPLY TEMP), AI (RETURN TEMP) TO FLOW COMPUTER.
 - ULTRASONIC FLOWMETER - SEE SPECIFICATIONS. CLAMP ON METER TYPE WITH REMOTE FLOW COMPUTER. COORDINATE WITH DIVISION 26 FOR 120V SINGLE-PHASE CIRCUIT FOR SELF-POWER CONTROLS. CONNECT FLOW COMPUTER TO DDC WITH AI (FLOW IN GPM), DI (FAULT), AI (TOTALIZATION), AI (SUPPLY CHW TEMP), AI (RETURN CHW TEMP), AI (INSTANTANEOUS BTU).
 - TEMPORARY CHILLER ISOLATION CONTROL VALVE WITH DO (OPEN/CLOSE) & DI (CLOSED POS.) SIGNALS TO DDC.
 - PRESSURE DIFFERENTIAL TRANSMITTER, PROVIDE AI (DIFF PRESS.) TO DDC. IMPULSE LINES SHALL BE MINIMUM 1/2" COPPER, B88, TYPE L. CONNECTIONS TO MAIN SHALL BE WITH DIELECTRIC UNION.
 - BUTTERFLY ISOLATION VALVES. PROVIDE WITH DEADEND SERVICE DESIGN AND BLIND FLANGE. INSTALL SYSTEM DRAIN AT PLANT SIDE OF VALVE. CONNECT SYSTEM DRAIN WITH 1-1/2" BY-PASS AS SHOWN FOR CHEMICAL TREATMENT AND CIRCULATION DURING PERIODS OF NON-USE.
 - TEMPORARY DDC PANEL - PROVIDE DDC PANEL LOCATED AS SHOWN ON THE PLANS. PANEL SHALL INCLUDE A BACKNET CONNECTION FOR TEMPORARY EQUIPMENT, AO (PUMP SPEED), DO (PUMP START STOP), DI (PUMP/VD FAULT), DI (CHILLER FAULT), AI (CHILLER CAPACITY), DI (CHILLER STATUS). PROVIDE SPARE IO TO INCLUDE 2 AI, 2 AO, 2 DI, AND 2 DO FOR USE AS NEEDED AT THE TIME OF RENTAL. BACKNET SHALL BE UTILIZED FOR PUMP SKID CONTROLLER, CHILLER CONTROLLER, AND ALL OTHER CONTROL PANELS LOCATED IN OR ON THE RENTAL TRAILER.
 - PROVIDE 1-1/2" BY-PASS AROUND MAIN ISOLATION VALVES AT PLANT HEADER. ONE BY-PASS SHALL BE A BALL VALVE. ONE BY-PASS SHALL BE A CALIBRATED BALANCE/CIRCUIT SETTER VALVE. MOUNT VALVES AT 5'-0" ABOVE FINISHED FLOOR, ON ADJACENT WALL. INITIAL SETTING SHALL BE 50 GPM. COORDINATE OFF-LINE TREATMENT FLOW WITH FACILITY WATER TREATMENT PROGRAM TO ACHIEVE PROPER CORROSION INHIBITOR AND BIOCIDES APPLICATION. TREATMENT FLOW WILL BE REVERSE OF NORMAL TEMPORARY CHILLED WATER FLOW.

A


B

C

D

E

F

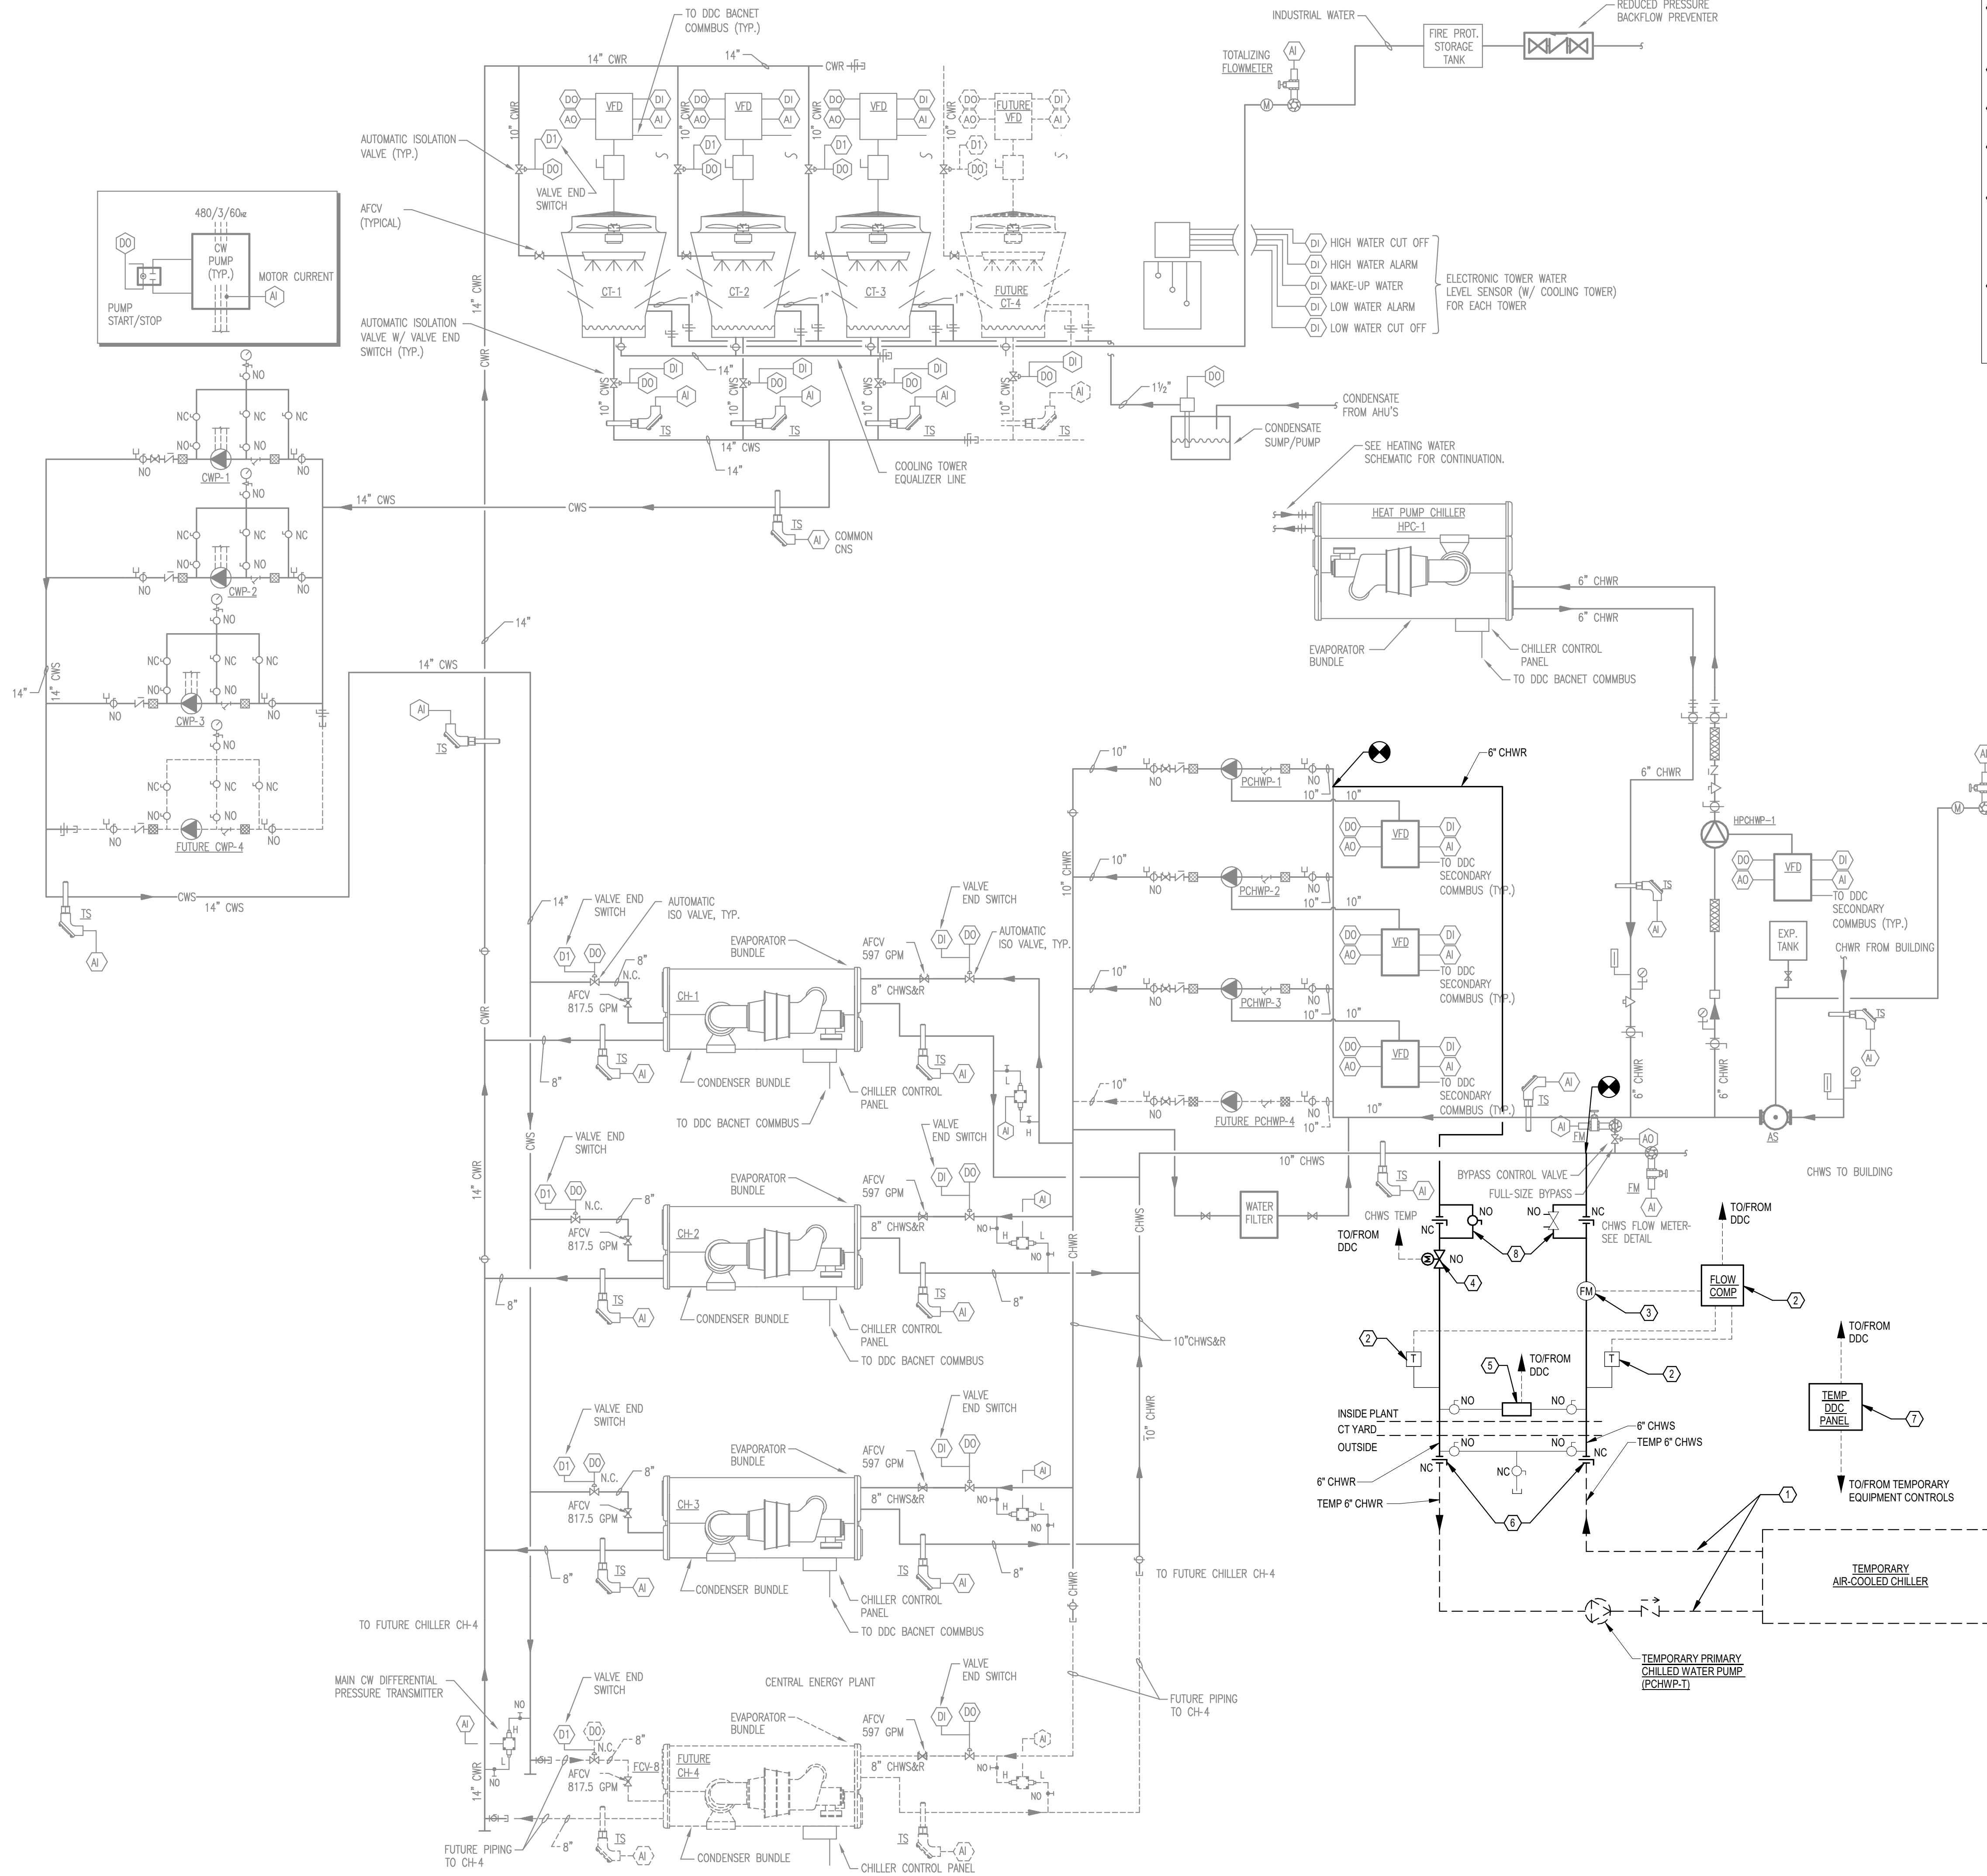

1 CHILLED WATER FLOW DIAGRAM
N.T.S.

CONSULTANT		ARCHITECT/ENGINEER OF RECORD		STAMP		Drawing Title		Phase		Project Title		Project Number	
						CHILLED WATER SYSTEM FLOW DIAGRAM		100% CONSTRUCTION DOCUMENTS		INSTALL ALTERNATE CONNECTIONS FOR STEAM AND CHILLED WATER		516-22-602	
						Approved:		FULLY SPRINKLERED		CAPE CORAL VA		Building Number	
										Location		Drawing Number	
										Issue Date		M-701	
										Checked			
										Drawn			
										RHA			
										WRH			

A

B

C

D


E

F

- | | |
|--|---|
| | <ol style="list-style-type: none"> 1. NATIONAL FIRE PROTECTION ASSOCIATION (NFPA), INCLUDING (BUT NOT LIMITED TO): <ol style="list-style-type: none"> a. NATIONAL ELECTRICAL CODE (NEC), NFPA 70- 2023 b. NATIONAL FIRE ALARM CODE, NFPA 72- 2022 c. LIFE SAFETY CODE, NFPA 101- 2021 d. EMERGENCY AND STANDBY POWER SYSTEMS, NFPA 110- 2022 e. HEALTH CARE FACILITIES CODE, NFPA 99 2. AMERICAN NATIONAL STANDARDS INSTITUTE (ANSI), INCLUDING (BUT NOT LIMITED TO): <ol style="list-style-type: none"> a. NATIONAL ELECTRICAL SAFETY CODE, ANSI C2 3. OCCUPATIONAL SAFETY AND HEALTH ACT (OSHA) 4. FEDERAL COMMUNICATION COMMISSION (FCC) 5. NATIONAL ELECTRICAL MANUFACTURERS ASSOCIATION (NEMA) 6. INSULATED CABLE ENGINEERS ASSOCIATION (ICEA) 7. INSTITUTE OF ELECTRICAL AND ELECTRONICS ENGINEERS (IEEE) 8. NATIONAL ELECTRICAL TESTING ASSOCIATION (NETA) 9. AMERICAN SOCIETY OF TESTING AND MATERIALS (ASTM) 10. ILLUMINATION ENGINEERING SOCIETY (IES) 11. ANTI-FRICTION BEARING MANUFACTURERS ASSOCIATION (AFBMA) 12. BUILDING OFFICIALS AND CODE ADMINISTRATORS INTERNATIONAL, INC. (BOCA) 13. INTERNATIONAL CODE COUNCIL (ICC): <ol style="list-style-type: none"> a. INTERNATIONAL BUILDING CODE (IBC) 14. UNIFORM BUILDING CODE (UBC) 15. COMBINED ASHRAE/IES STANDARD 90.1- "ENERGY STANDARD FOR BUILDINGS EXCEPT LOW-RISE RESIDENTIAL BUILDINGS" 16. NATIONAL ELECTRICAL CONTRACTORS ASSOCIATION INSTALLATION STANDARDS (NECA) 17. AMERICANS WITH DISABILITIES ACT (ADA) 18. APPLICABLE STATE AND LOCAL CODES, AMENDMENTS, REGULATIONS, AND PRACTICES. 19. APPLICABLE REGULATORY REQUIREMENTS AND ADVISORY PRACTICES OF APPROPRIATE <ol style="list-style-type: none"> a. AUTHORITIES HAVING JURISDICTION (AHJs). 20. APPLICABLE STANDARDS, REGULATIONS, AND PRACTICES OF THE OWNER. |
|--|---|



F

VA FORM 08-6231									
1	2	3	4	5	6	7	8	9	10

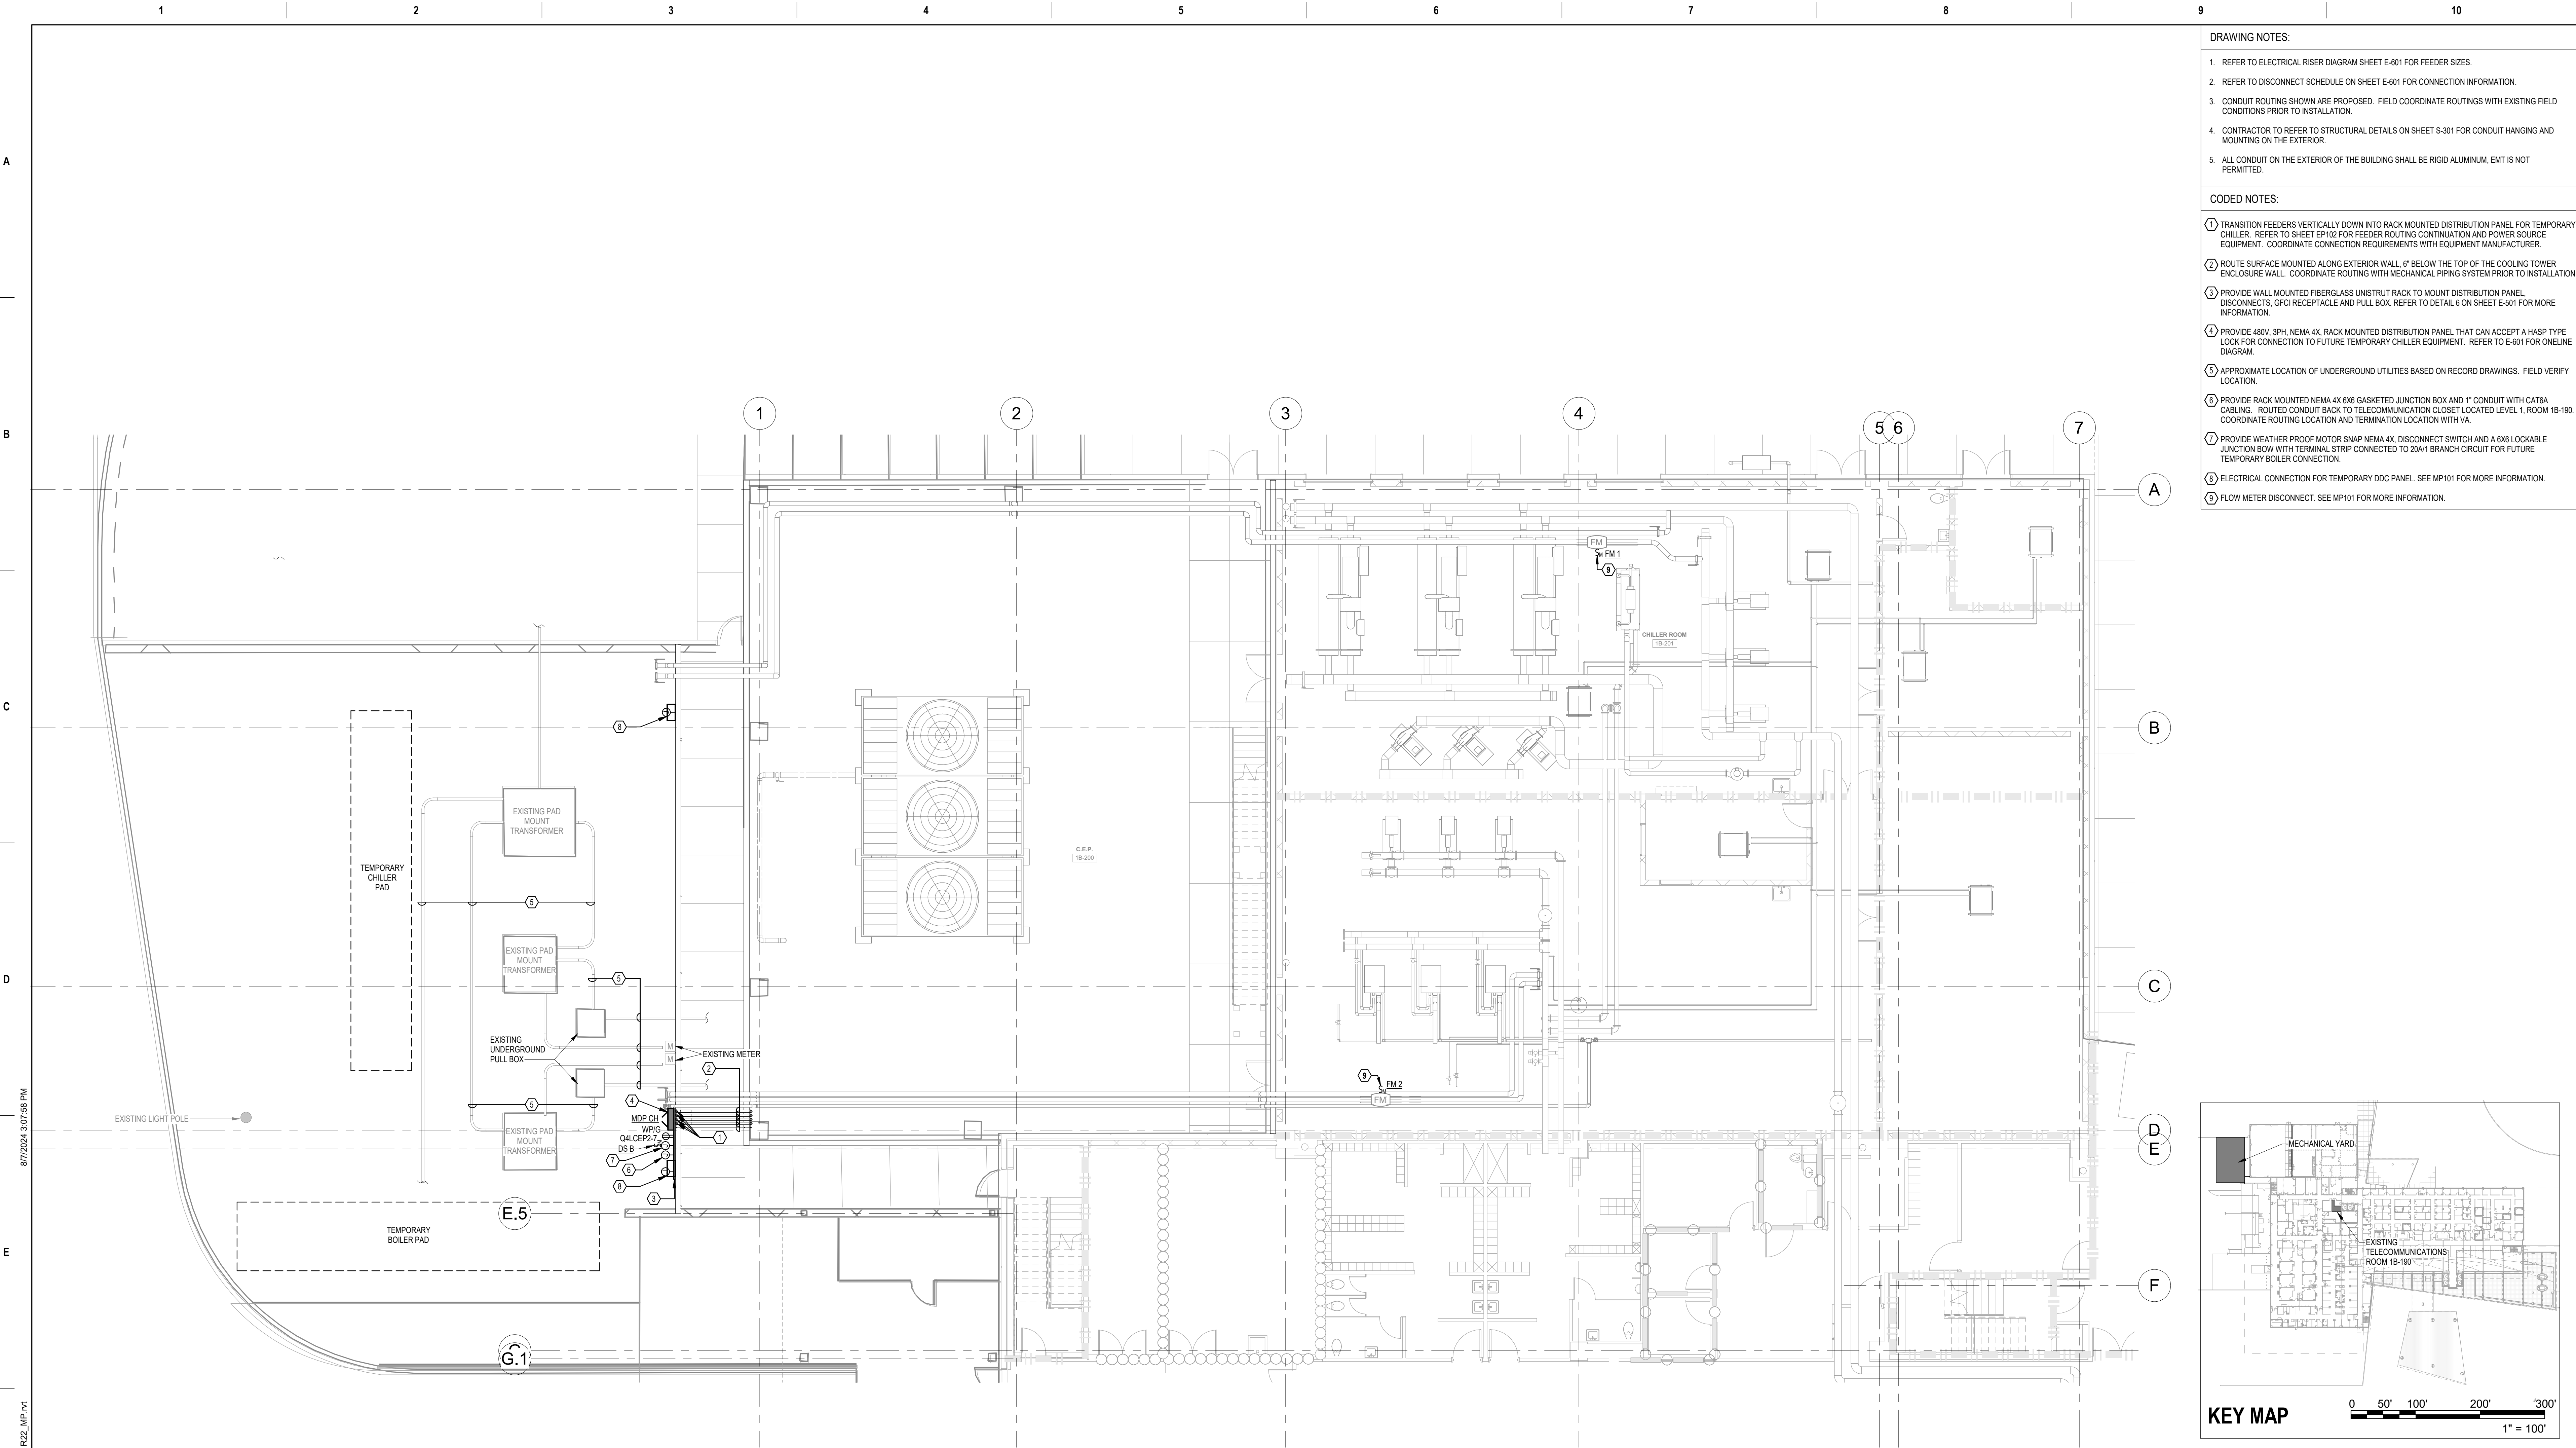

1 FLOOR PLAN - ELECTRICAL- NEW WORK - LEVEL 1
1/8" = 1'-0"

- DRAWING NOTES:
1. REFER TO ELECTRICAL RISER DIAGRAM SHEET E-601 FOR FEEDER SIZES.
 2. REFER TO DISCONNECT SCHEDULE ON SHEET E-601 FOR CONNECTION INFORMATION.
 3. CONDUIT ROUTING SHOWN ARE PROPOSED. FIELD COORDINATE ROUTINGS WITH EXISTING FIELD CONDITIONS PRIOR TO INSTALLATION.
 4. CONTRACTOR TO REFER TO STRUCTURAL DETAILS ON SHEET S-301 FOR CONDUIT HANGING AND MOUNTING ON THE EXTERIOR.
 5. ALL CONDUIT ON THE EXTERIOR OF THE BUILDING SHALL BE RIGID ALUMINUM. EMT IS NOT PERMITTED.
- CODED NOTES:
- 1 TRANSITION FEEDERS VERTICALLY DOWN INTO RACK MOUNTED DISTRIBUTION PANEL FOR TEMPORARY CHILLER. REFER TO SHEET EP102 FOR FEEDER ROUTING CONTINUATION AND POWER SOURCE EQUIPMENT. COORDINATE CONNECTION REQUIREMENTS WITH EQUIPMENT MANUFACTURER.
 - 2 ROUTE SURFACE MOUNTED ALONGS EXTERIOR WALL, 6" BELOW THE TOP OF THE COOLING TOWER ENCLOSURE WALL. COORDINATE ROUTING WITH MECHANICAL PIPING SYSTEM PRIOR TO INSTALLATION.
 - 3 PROVIDE WALL MOUNTED FIBERGLASS UNISTRUT RACK TO MOUNT DISTRIBUTION PANEL DISCONNECTS, GFCI RECEPTACLE AND PULL BOX. REFER TO DETAIL 6 ON SHEET E-601 FOR MORE INFORMATION.
 - 4 PROVIDE 480V, 3PH, NEMA 4X, RACK MOUNTED DISTRIBUTION PANEL THAT CAN ACCEPT A HASP TYPE LOCK FOR CONNECTION TO FUTURE TEMPORARY CHILLER EQUIPMENT. REFER TO E-601 FOR ONLINE DIAGRAM.
 - 5 APPROXIMATE LOCATION OF UNDERGROUND UTILITIES BASED ON RECORD DRAWINGS. FIELD VERIFY LOCATION.
 - 6 PROVIDE RACK MOUNTED NEMA 4X 6X6 GASKETED JUNCTION BOX AND 1" CONDUIT WITH CAT6A CABLE. ROUTED CONDUIT BACK TO TELECOMMUNICATION CLOSET LOCATED LEVEL 1, ROOM 18-190. COORDINATE ROUTING LOCATION AND TERMINATION LOCATION WITH VA.
 - 7 PROVIDE WEATHER PROOF MOTOR SNAP NEMA 4X, DISCONNECT SWITCH AND A 6X6 LOCKABLE JUNCTION BOX WITH TERMINAL STRIP CONNECTED TO 20A1 BRANCH CIRCUIT FOR FUTURE TEMPORARY BOILER CONNECTION.
 - 8 ELECTRICAL CONNECTION FOR TEMPORARY DDC PANEL. SEE MP101 FOR MORE INFORMATION.
 - 9 FLOW METER DISCONNECT. SEE MP101 FOR MORE INFORMATION.

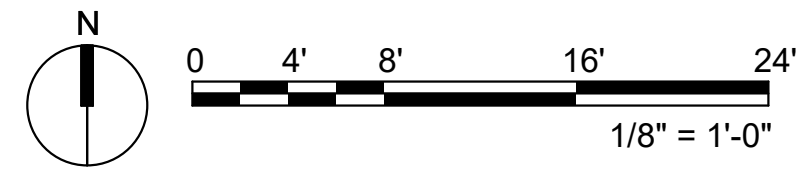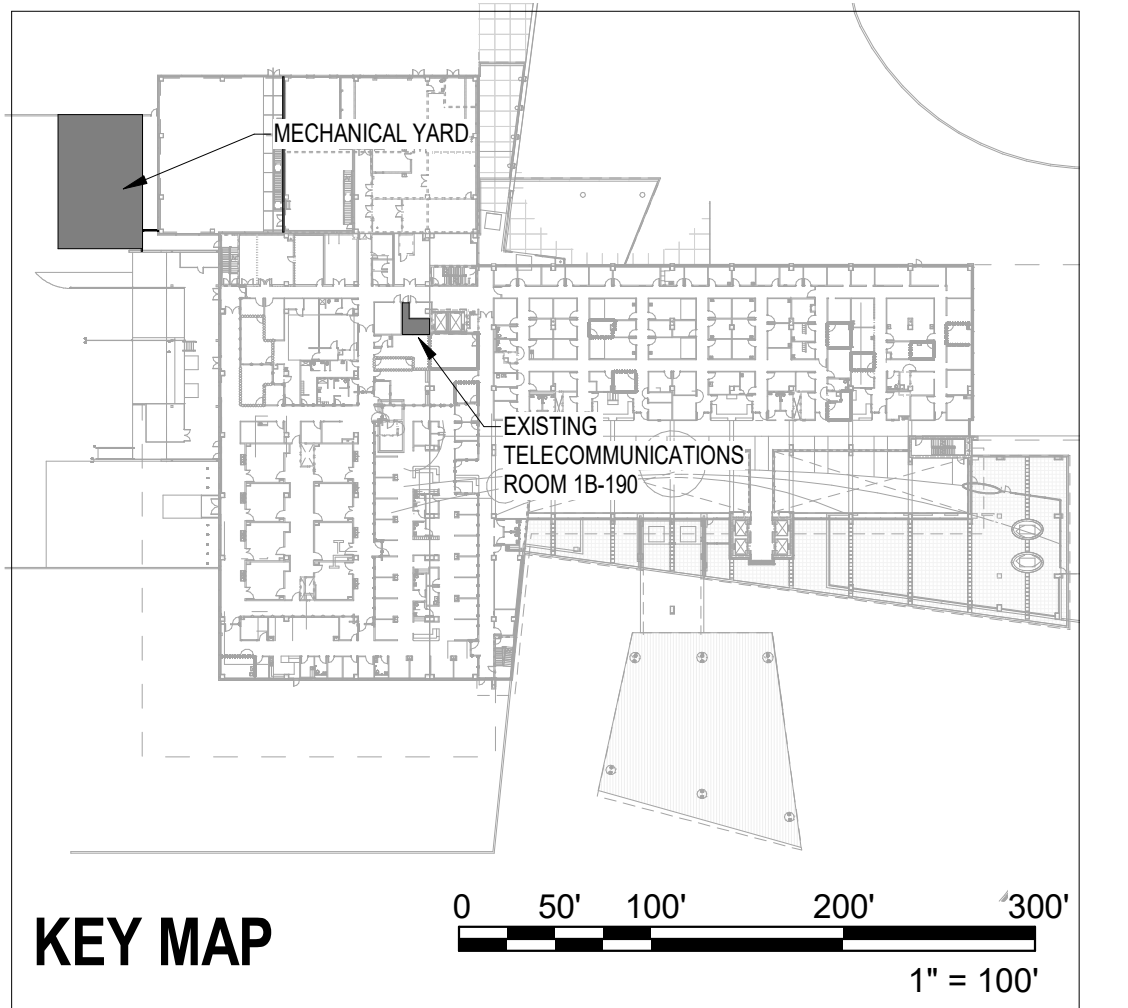

		CONSULTANT	ARCHITECT/ENGINEER OF RECORD		STAMP	Office of Construction and Facilities Management		Drawing Title		Phase	Project Title		Project Number	
						U.S. Department of Veterans Affairs		FLOOR PLAN - ELECTRICAL- NEW WORK - LEVEL 1			INSTALL ALTERNATE CONNECTIONS FOR STEAM AND CHILLED WATER		516-22-602	
								Approved:		FULLY SPRINKLERED	Location		Drawing Number	
									CAPE CORAL VA			EP101		
											Issue Date		Checked	
											08/07/2024		BMS	
													Drawn	
													KEM	

- 1 SECOND FLOOR PLAN - ELECTRICAL - NEW WORK
1/8" = 1'-0"




EP102



www.abovegroupinc.com
COA/CA Lic. No. 31120

**305 East Dr., Suite H,
Melbourne, Florida 32904
PH: 321.345.9026**

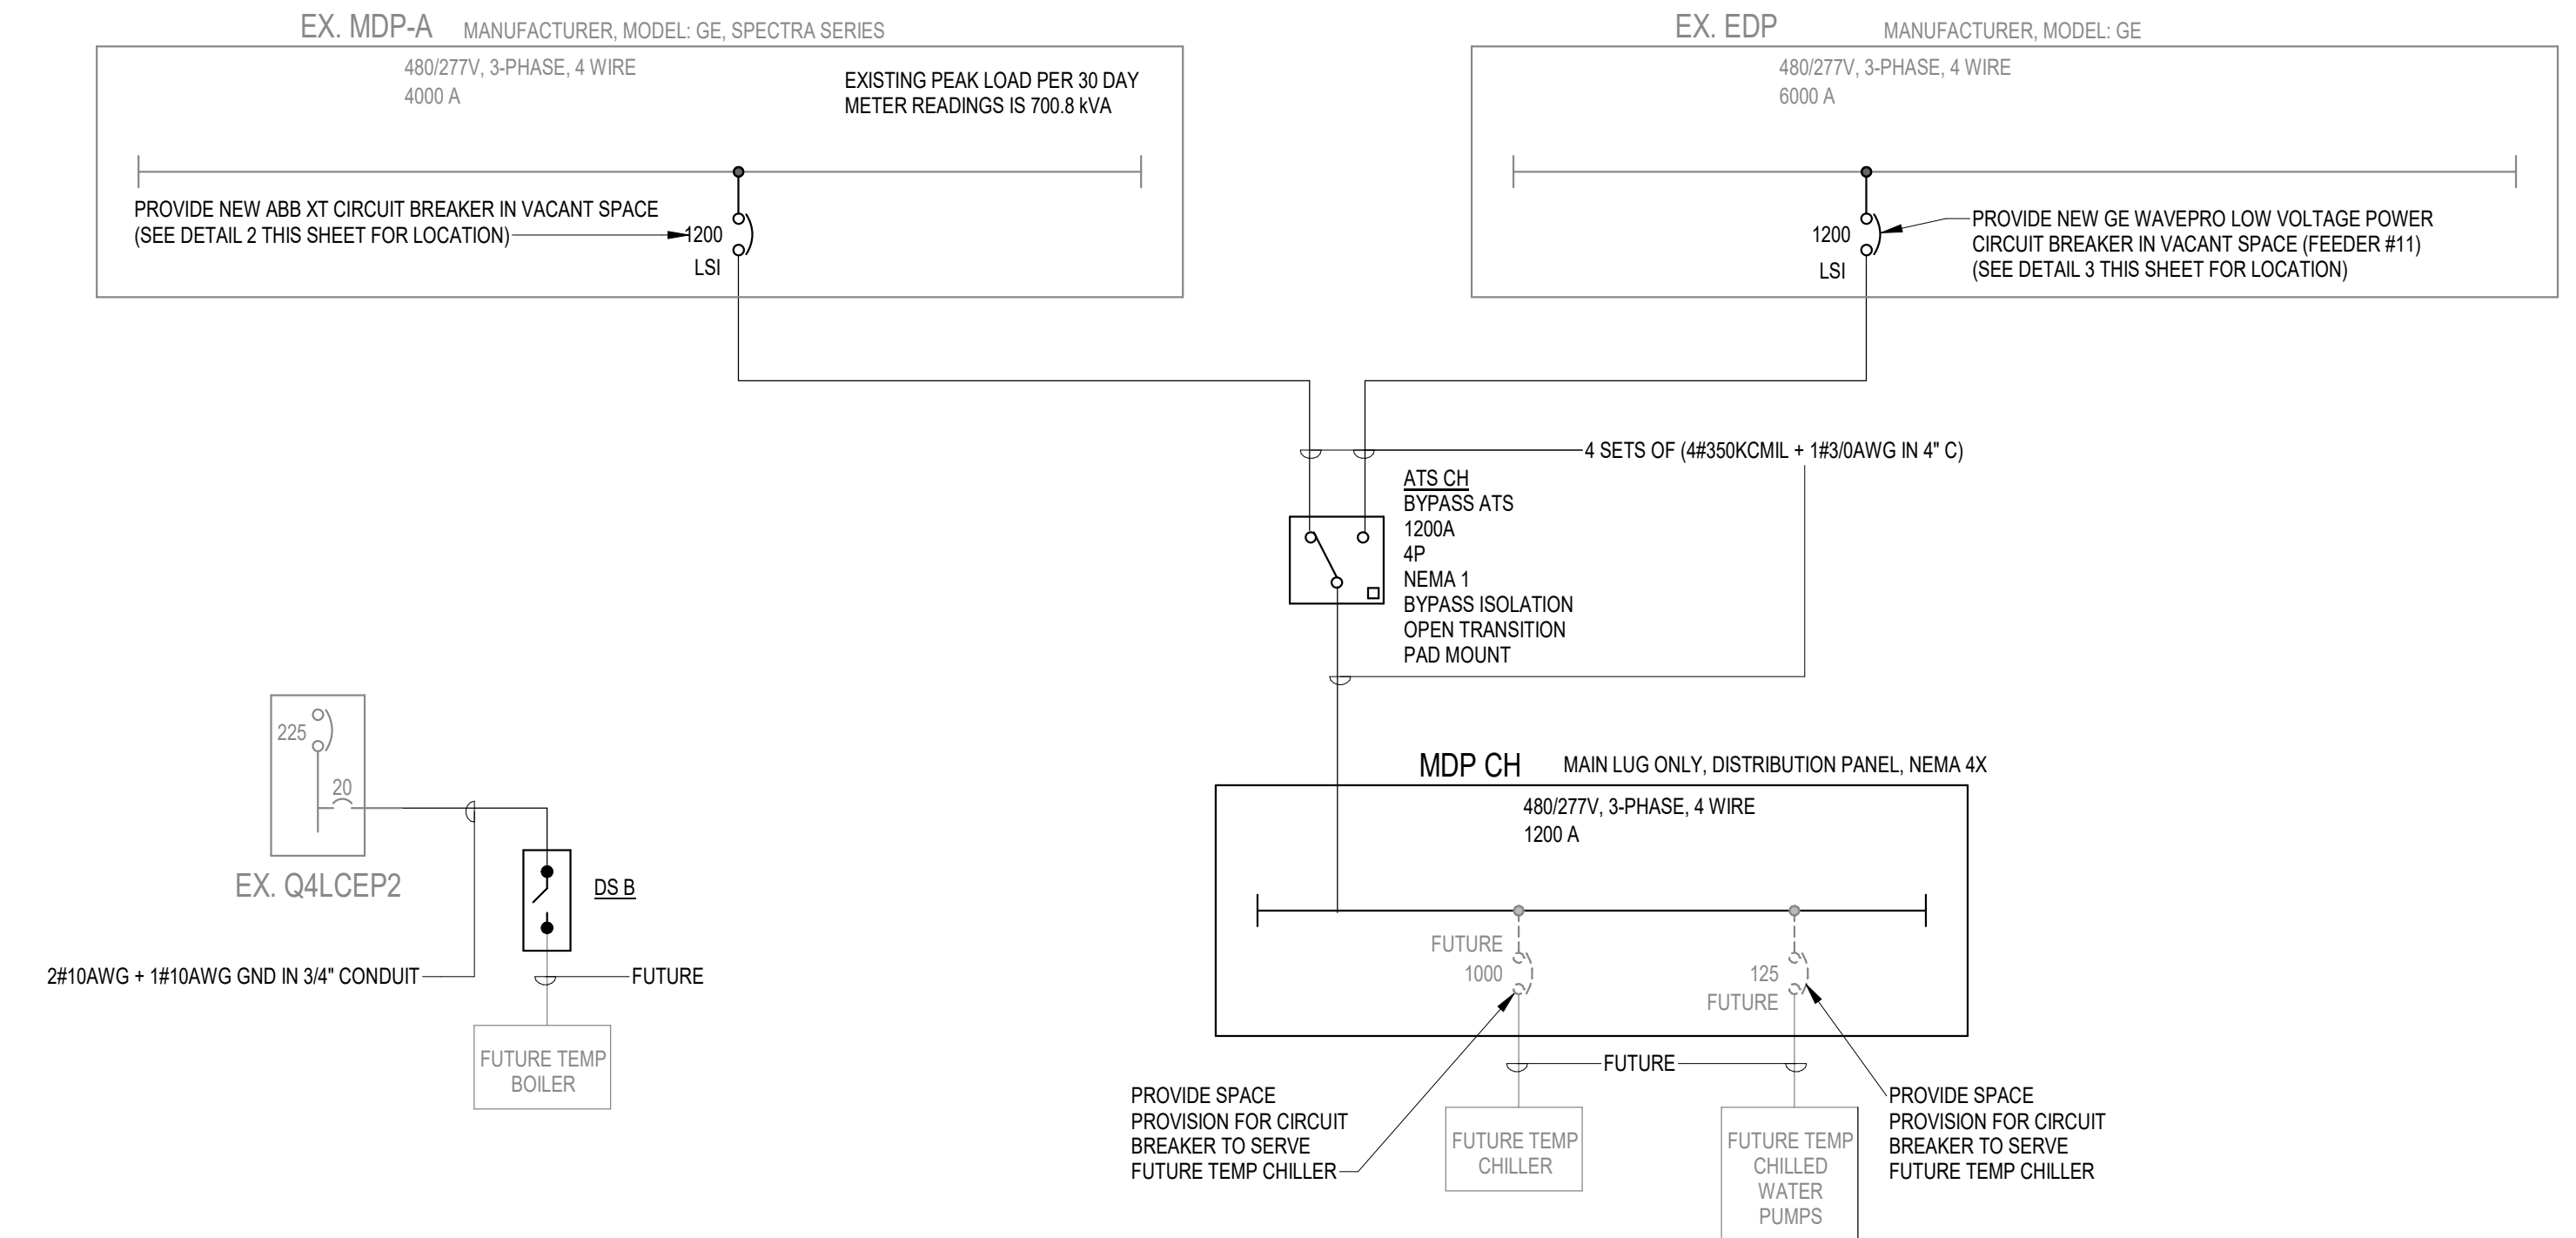

DISCONNECT SCHEDULE							
DISC NAME	TYPE OF EQUIPMENT	VOLTAGE RATING	ENCLOSURE RATING	DISC. AMP/POLE	FUSE/BREAKER SIZE	STARTER SIZE	DISCONNECT NOTES
DS 8	MOTOR RATED SNAP SWITCH	120V	NEMA 4X	20A/1P	N/A	N/A	
FM 1	MOTOR RATED SNAP SWITCH	120V	NEMA 1	20A/1P	N/A	N/A	
FM 2	MOTOR RATED SNAP SWITCH	120V	NEMA 1	20A/1P	N/A	N/A	

EXISTING PANEL: Q4LCEP2

LOCATION: 2B-196

SUPPLY FROM: TQ4LCEP2

MOUNTING: Surface

ENCLOSURE: Type 1

VOLTS: 120/208 Vlye

PHASES: 3

WIRES: 4

A.I.C. RATING: 10000

MAINS TYPE: MCB

MAINS RATING: 225 A

SERVICE ENTRANCE: No

GENERAL NOTES:

1. 2 SECTION PANEL

2. PANEL MANUFACTURER, MODEL: GENERAL ELECTRIC, AQ

CKT	CIRCUIT DESCRIPTION	NOTE S	TRIP	POLES	A	B	C	POLES	TRIP	NOTE S	CIRCUIT DESCRIPTION	CKT	
1	EX. FCU 2-4		15 A	1	1500... 1500...			1	15 A		EX. FCU 2-3	2	
3	EX. FCU 2-2A		15 A	1		1500... 1500...		1	15 A		EX. FCU 2-6	4	
5	EX. FCU 2-1		15 A	1			1500... 100 VA	1	20 A		EX. GENERATOR DAYTANK CTRL# 3	6	
7	EXTIORIOR RECEPTACLE	1	20 A	1	180 VA 100 VA			1	20 A		EX. GENERATOR DAYTANK CTRL# 82	8	
9	FUTURE BOILER	1	20 A	1		500 VA 100 VA		1	20 A		EX. GENERATOR DAYTANK CTRL# 1	10	
11	TEMPORARY DDC PANEL	1	20 A	1			500 VA 0 VA	1	20 A		EX. SPARE	12	
13	EX. GAS WATER HEATER #3		20 A	1	1200... 0 VA			1	20 A		EX. SPARE	14	
15	EX. GAS WATER HEATER #2		20 A	1		0 VA 0 VA		1	20 A		EX. SPARE	16	
17	EX. GAS WATER HEATER #1		20 A	1			0 VA 0 VA	1	20 A		EX. SPARE	18	
19	EX. WATER TREATMENT		20 A	1	1200... 1200...			1	20 A		EX. SPARE	20	
21	EX. RP-1		15 A	1		0 VA 0 VA		1	20 A		EX. SPARE	22	
23	EX. REFRIGERANT MONITOR PANEL		15 A	1			0 VA 0 VA	1	20 A		EX. SPARE	24	
25	EX. REC WATER TREATMENT		20 A	1	180 VA 0 VA			1	20 A		EX. SPARE	26	
27	EX. SPARE		20 A	1		0 VA 1200...		1	20 A		EX. UNIT HEATER	28	
29	EX. B-2		20 A	1			1200... 1200...	1	20 A		EX. UNIT HEATER	30	
31	EX. B-1		20 A	1	1200... 100 VA			1	15 A		EX. FUEL PUMP	32	
33	TEMPORARY DDC PANEL	1	20 A	1		500 VA 100 VA		1	15 A		EX. FUEL PUMP	34	
35	FLOW METER	1	20 A	1			20 VA 100 VA	1	15 A		EX. FUEL PUMP	36	
37	FLOW METER	1	20 A	1	20 VA 100 VA			1	15 A		EX. FUEL PUMP	38	
39	EX. SPARE		15 A	1		0 VA 100 VA		1	20 A		EX. DDC CONTROL PANEL	40	
41	EX. SPARE		20 A	1			0 VA 100 VA	1	20 A		EX. DDC CONTROL PANEL	42	
43	EX. #1 COOLING TOWER CONTROL PANEL		20 A	1	100 VA 1500...			3	20 A			44	
45	EX. #2 COOLING TOWER CONTROL PANEL		20 A	1		100 VA 1500...					EX. HWCP -3 BOILER	46	
47	EX. #3 COOLING TOWER CONTROL PANEL		20 A	1			100 VA 1500...					48	
49	EX. SPARE		20 A	2	0 VA 1500...			3	20 A			50	
51						0 VA 1500...					EX. HWCP 3 PUMP	52	
53	EX. B-2 POWER		20 A	2	1500... 100 VA		1500... 1500...	1	20 A		EX. DDC CONTROL PANEL	56	
57	EX. B-1 POWER		20 A	2		1500... 0 VA		1	20 A		EX. SPARE	58	
59							1500... 100 VA	1	20 A		EX. DDC CONTROL PANEL	60	
61	EX. SPARE		20 A	1	0 VA 100 VA			62	20 A		EX. CHEM. WATER TRMT	62	
63	EX. SPARE		20 A	1		0 VA 100 VA		1	20 A		EX. CHEM. WATER TRMT	64	
65	EX. NAT. CABINET MAIN		20 A	1			100 VA 0 VA	1	20 A		EX. SPARE	66	
67	EX. NAT. CABINET MAIN		20 A	1	100 VA 1500...			3	20 A			68	
69	EX. NAT. CABINET MAIN		20 A	1		100 VA 1500...					EX. R/O WATER	70	
71	EX. FUEL TRANSFER PUMP		20 A	1			100 VA 1500...					72	
73	EX. SPARE		20 A	1	0 VA 0 VA			1	20 A		EX. SPARE	74	
75	EX. SPARE		20 A	1		0 VA 0 VA		1	20 A		EX. SPARE	76	
77	EX. WATER HEATER PANEL		20 A	1			100 VA 500 VA	1	20 A		EX. FUEL MAINTENANCE	78	
79	EX. SPARE		20 A	1	0 VA 200 VA			1	20 A		EX. WATER TREATMENT	80	
81	EX. FCU 2-4		20 A	1		1500... 1200...		1	20 A		EX. GENERATOR LOUVERS	82	
83	EX. FCU 2-6		20 A	1			1500... 0 VA	1	20 A		EX. SPARE	84	
					TOTAL...	15044 VA	14500 VA	14720 VA					
					TOTAL...	126 A	121 A	123 A					

LEGEND:

LOAD CLASSIFICATION	CONNECTED LOAD	DEMAND FACTOR	ESTIMATED DEMAND	PANEL TOTALS
Other	1540 VA	100.00%	1540 VA	TOTAL CONNECTED LOAD: 44264 VA TOTAL EST. DEMAND: 54909 VA TOTAL CONNECTED... 123 A TOTAL EST. DEMAND... 152 A
Receptacle	180 VA	100.00%	180 VA	
Spare	42580 VA	125.00%	53225 VA	

BRANCH CIRCUIT NOTES:

1. CONNECT TO EXISTING SPARE 20A 1 POLE BREAKER.

[illegible]