


P
O
N
M
L
K
J
I
H
G
F
E
D
C
B
A

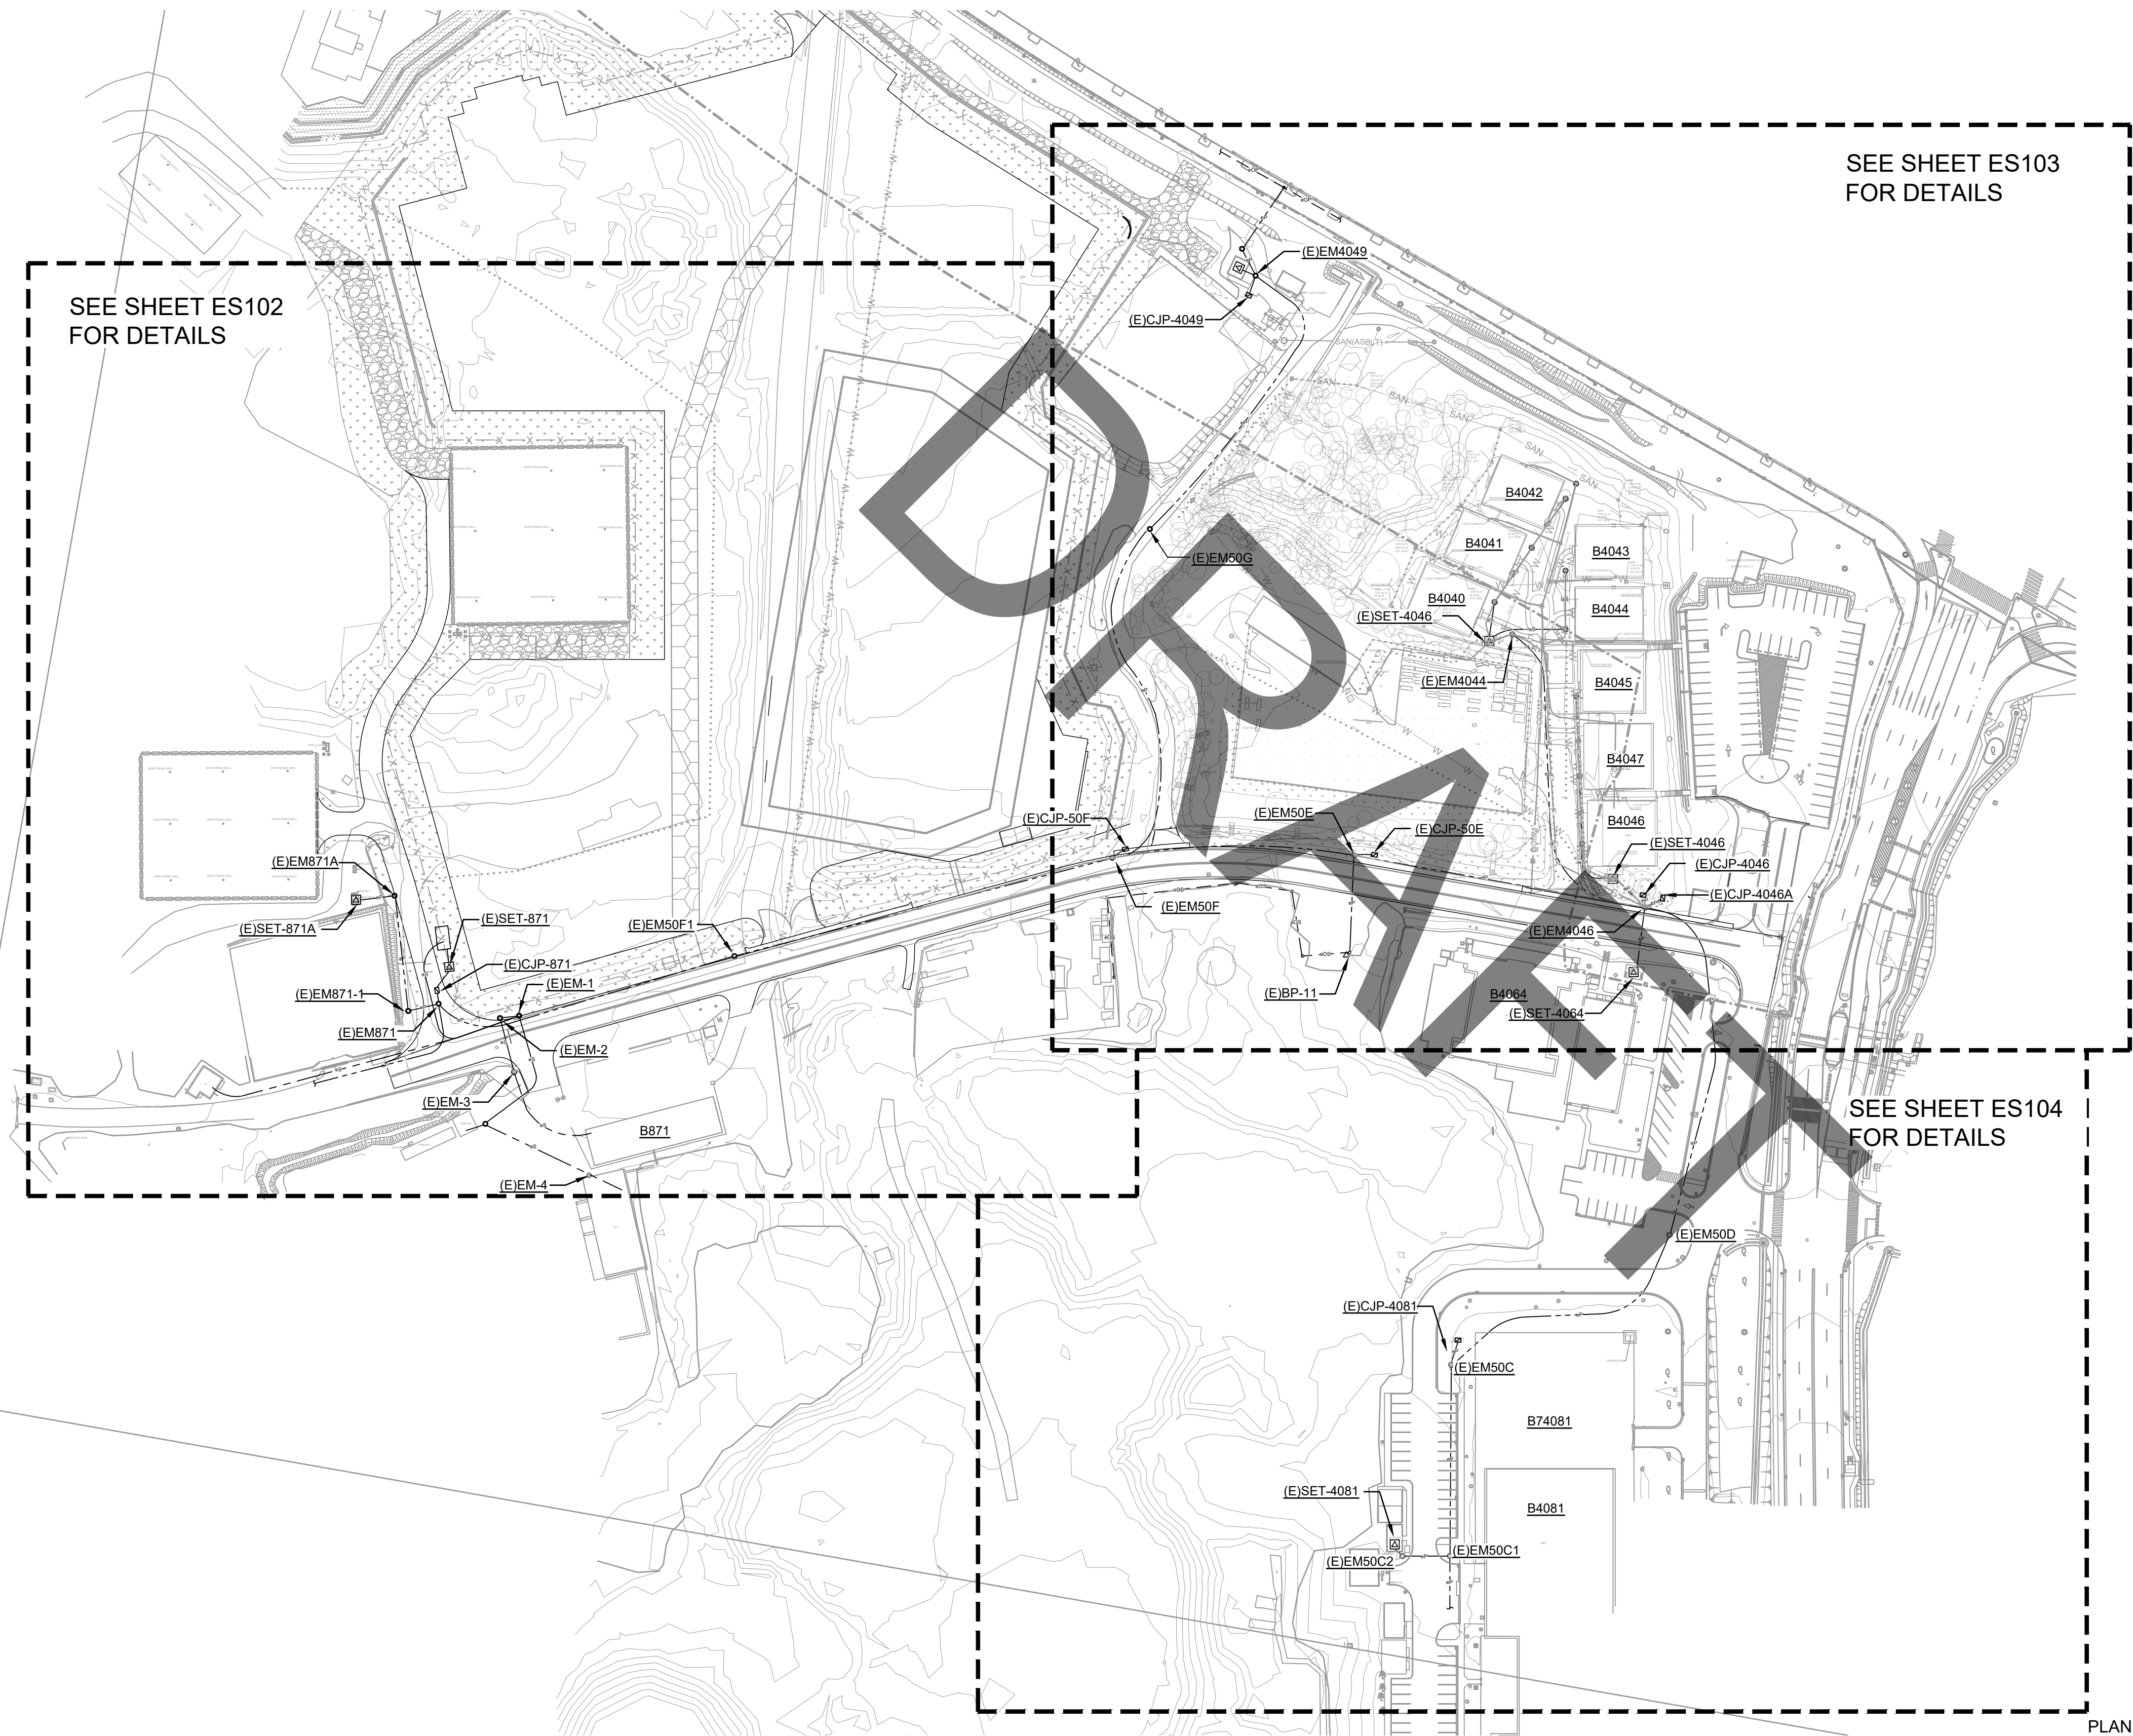

A1 OVERALL SITE ELECTRICAL DEMOLITION PLAN (CLIN0001-CLIN0003)
1:1000

GENERAL NOTES

1. SEE CIVIL AND TELECOMMUNICATIONS PLANS FOR SITE DEMOLITION WORK AND CLOSELY COORDINATE THE ELECTRICAL DEMOLITION WORK.
2. PRIOR TO ANY ELECTRICAL EQUIPMENT AND INFRASTRUCTURE DEMOLITION WORK, ENSURE THAT THE NEW EQUIPMENT AND INFRASTRUCTURE ARE ESTABLISHED TO MINIMIZE DISRUPTION TO THE OPERATIONS OF THE EXISTING FACILITIES.
3. THE CONTRACTOR SHALL BE RESPONSIBLE TO SUBMIT A PROPOSED PHASING SCHEME IN COORDINATION WITH CIVIL AND TELECOMMUNICATIONS WORK FOR REVIEW AND APPROVAL PRIOR TO START OF DEMOLITION WORK.


KEY NOTES

CLIN 0001-0003

- CLIN 0001:**
- SITE PREPARATION WORK FOR VMS FACILITIES.
 - LOONEY STREET AND ELECTRICAL INFRASTRUCTURE IMPROVEMENTS.
 - RELOCATE CJP AND TRANSFORMER SERVING B871 (RECYCLING FACILITY) AND OTHER BUILDINGS.
 - CONSTRUCTION OF VEHICLE MAINTENANCE SHOP, FIRE PUMP HOUSE, WATER STORAGE TANK, CABLE HUT, AND ASSOCIATED ELECTRICAL INFRASTRUCTURE.

- CLIN 0002:**
- CONSTRUCTION OF ORGANIZATIONAL EQUIPMENT STORAGE, POL STORAGE, AND ASSOCIATED ELECTRICAL INFRASTRUCTURE.

- CLIN 0003:**
- CONSTRUCTION OF ORGANIZATIONAL VEHICLE PARKING LOT AND SITE LIGHTING.
 - CONSTRUCTION OF WASH RACK AND ASSOCIATED ELECTRICAL INFRASTRUCTURE.

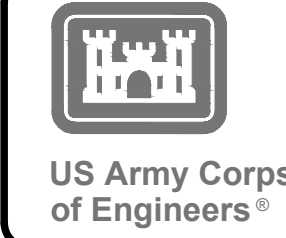


MARK	DESCRIPTION	DATE

DESIGNED BY:	ISSUE DATE:
DRAWN BY:	SOLICITATION NO.:
CHECKED BY:	CONTRACT NO.:
SUBMITTED BY:	SCALE:
SIZE:	FILE NAME:
ISO A1	AS SHOWN
US ARMY CORPS OF ENGINEERS JAPAN DISTRICT, OKINAWA AREA OFFICE USAED-J UNIT 35132 APO, AP 96374-5132 SSFM SSFM INTERNATIONAL, INC. 501 SUMNER STREET, SUITE 620 HONOLULU, HAWAII 96817	

KADENA AIR BASE, OKINAWA, JAPAN
VEHICLE MAINTENANCE SHOP
FY20 MCA PN77833
OVERALL SITE ELECTRICAL DEMOLITION PLAN (CLIN 0001 - CLIN 0003)

SHEET ID
ES101

INTERMEDIATE DESIGN

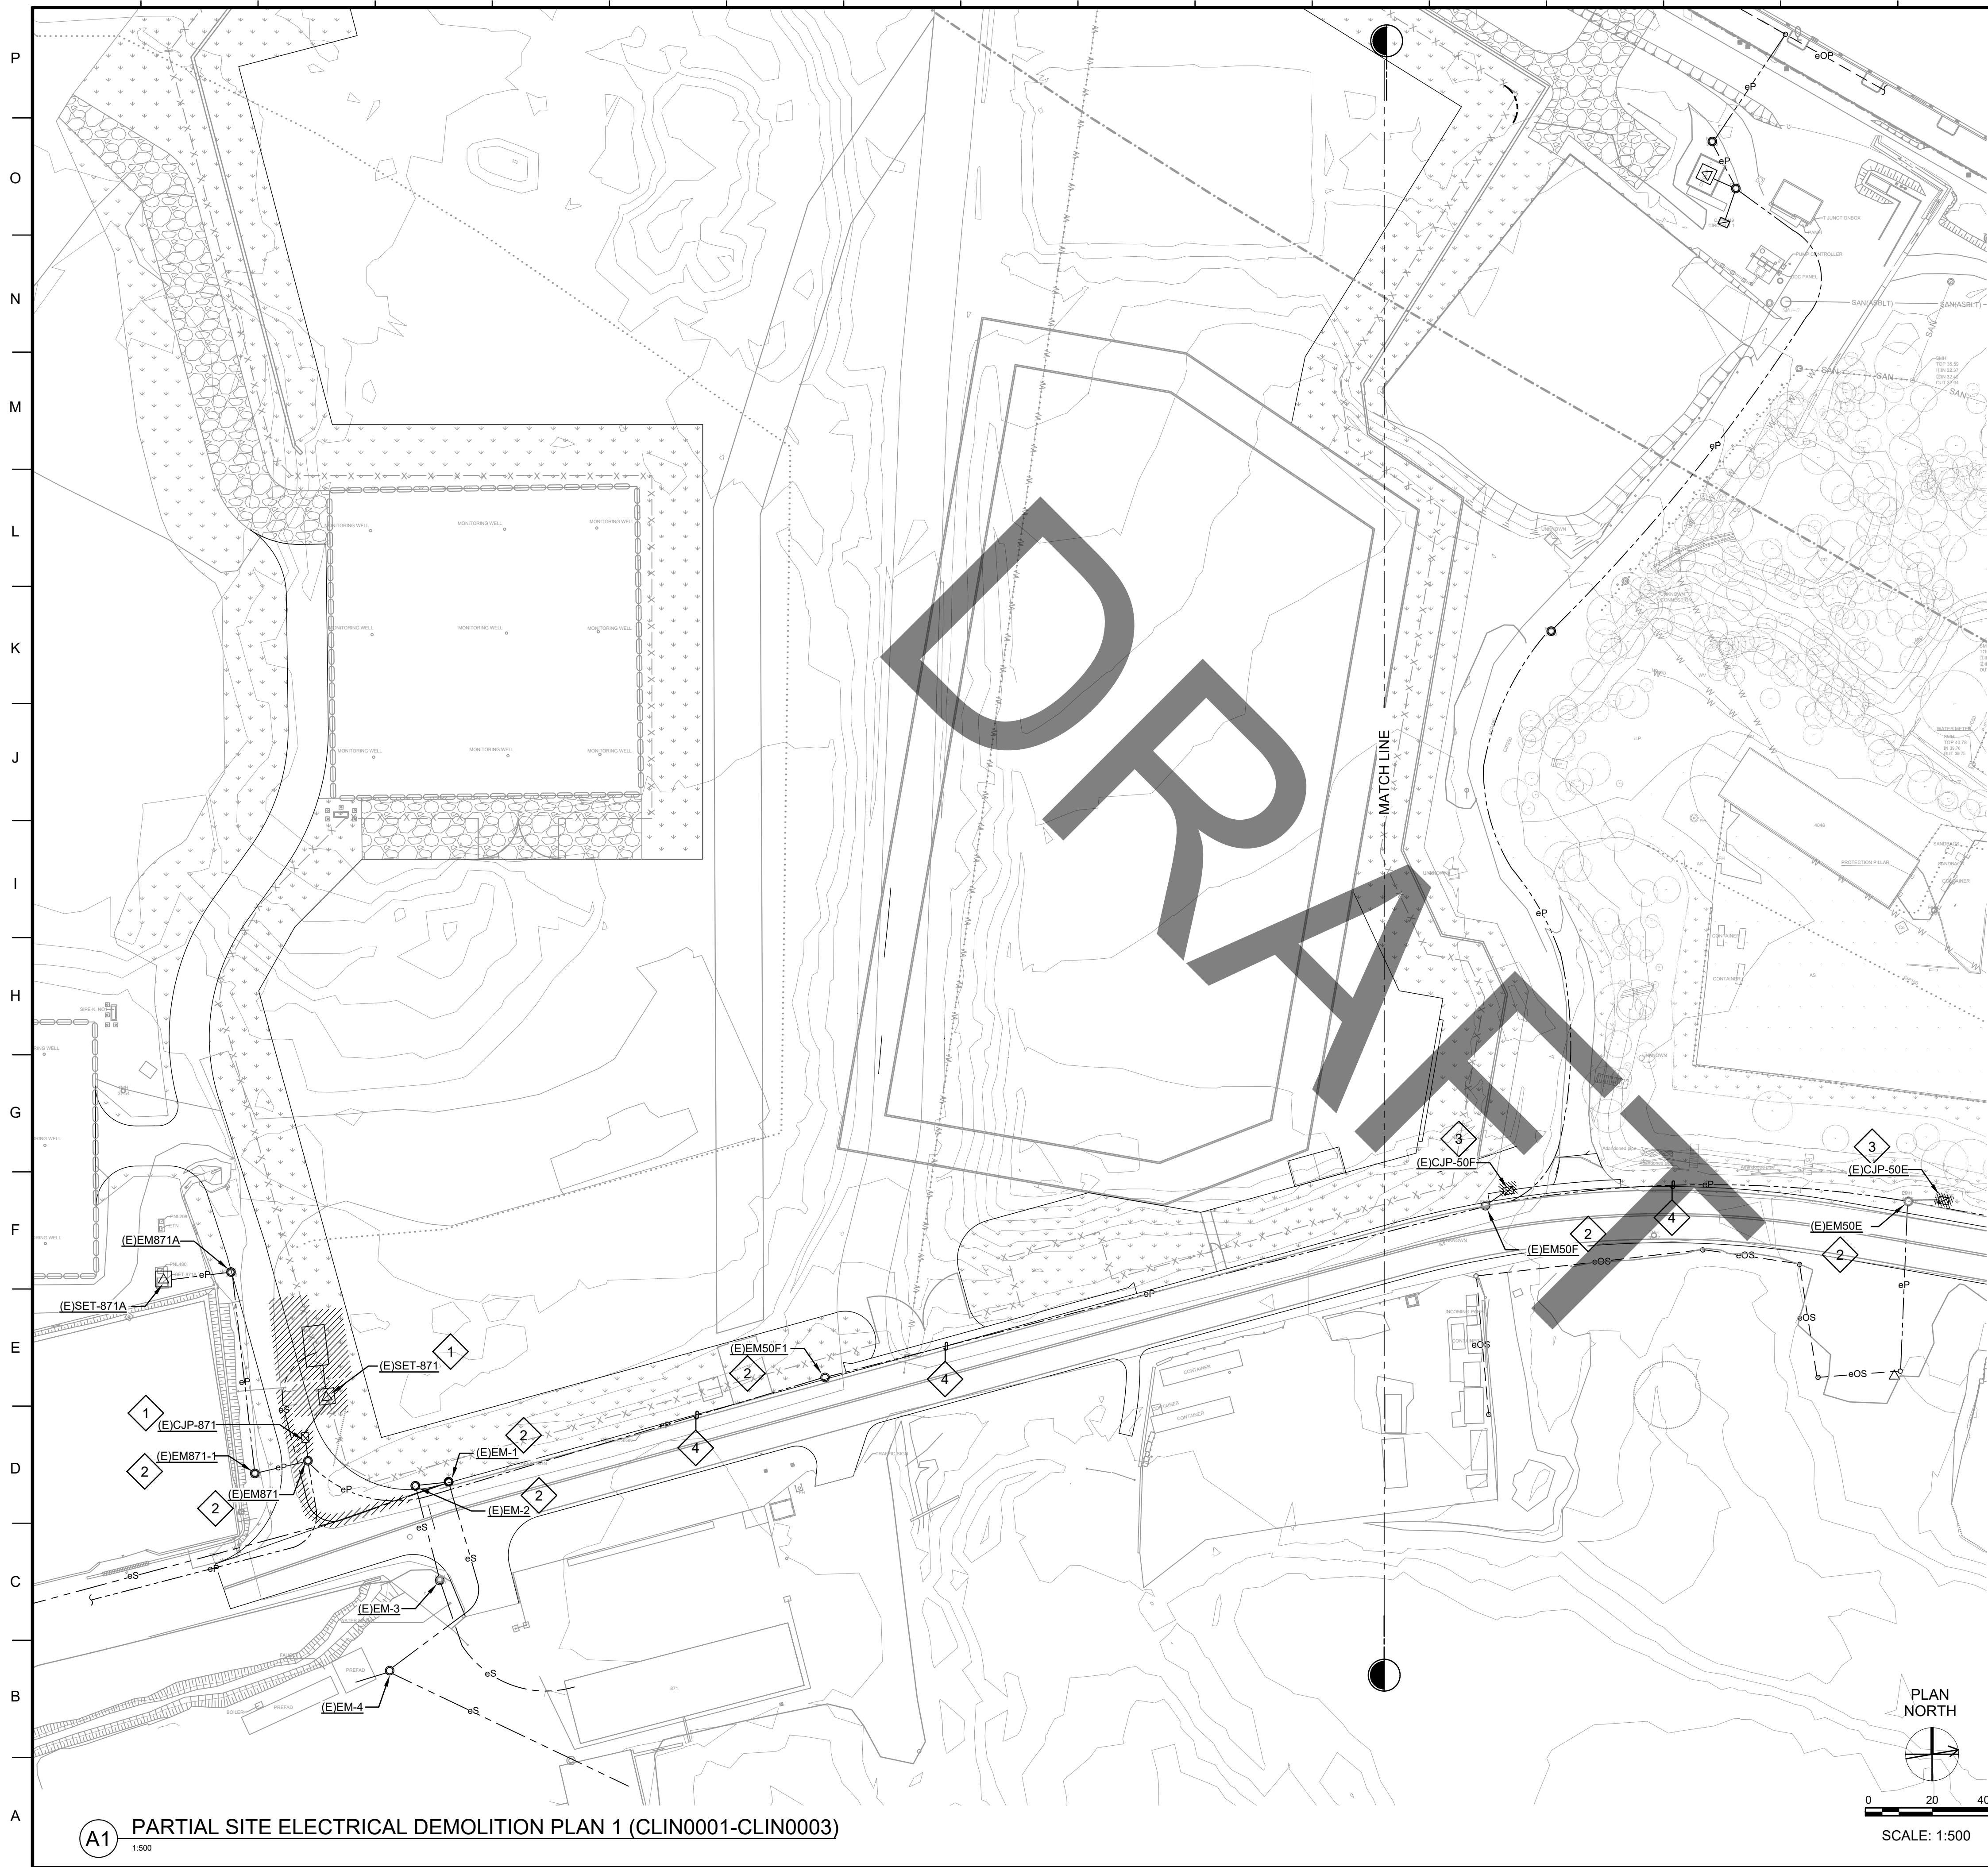

GENERAL NOTES

1. SEE CIVIL AND TELECOMMUNICATIONS PLANS FOR SITE DEMOLITION WORK AND CLOSELY COORDINATE THE ELECTRICAL DEMOLITION WORK.
2. PRIOR TO ANY ELECTRICAL EQUIPMENT AND INFRASTRUCTURE DEMOLITION WORK, ENSURE THAT THE NEW EQUIPMENT AND INFRASTRUCTURE ARE ESTABLISHED TO MINIMIZE DISRUPTION TO THE OPERATIONS OF THE EXISTING FACILITIES.
3. THE CONTRACTOR SHALL BE RESPONSIBLE TO SUBMIT A PROPOSED PHASING SCHEME IN COORDINATION WITH CIVIL AND TELECOMMUNICATIONS WORK FOR REVIEW AND APPROVAL PRIOR TO START OF DEMOLITION WORK.

KEY NOTES

1. EXISTING CJP-871, SET-871, DISTRIBUTION EQUIPMENT AND ASSOCIATED FEEDERS SHALL BE DEMOLISHED AND RELOCATED TO ACCOMMODATE THE ORGANIZATIONAL VEHICLE PARKING AND ACCESS ROAD REALIGNMENT.
2. EXISTING MANHOLES SHALL BE SALVAGED AND REUSED. MODIFY MANHOLE FINISH TO MATCH THE FINAL GRADING.
3. EXISTING CJP SHALL BE REMOVED AND REPLACED WITH NEW TO RESTORE SERVICES TO EXISTING FACILITIES AND TO FACILITATE NEW SERVICES TO THE PROPOSED BUILDINGS.
4. EXISTING PRIMARY FEEDER SHALL BE REMOVED AND REPLACED AND EXISTING DUCTS WILL BE UTILIZED AS A TEMPORARY SERVICE OR REMAIN AS A SPARE.

CLIN 0001-0003

- CLIN 0001:**
- SITE PREPARATION WORK FOR VMS FACILITIES.
 - LOONEY STREET AND ELECTRICAL INFRASTRUCTURE IMPROVEMENTS.
 - RELOCATE CJP AND TRANSFORMER SERVING B871 (RECYCLING FACILITY) AND OTHER BUILDINGS.
 - CONSTRUCTION OF VEHICLE MAINTENANCE SHOP, FIRE PUMP HOUSE, WATER STORAGE TANK, CABLE HUT, AND ASSOCIATED ELECTRICAL INFRASTRUCTURE.
- CLIN 0002:**
- CONSTRUCTION OF ORGANIZATIONAL EQUIPMENT STORAGE, POL STORAGE, AND ASSOCIATED ELECTRICAL INFRASTRUCTURE.
- CLIN 0003:**
- CONSTRUCTION OF ORGANIZATIONAL VEHICLE PARKING LOT AND SITE LIGHTING.
 - CONSTRUCTION OF WASH RACK AND ASSOCIATED ELECTRICAL INFRASTRUCTURE.

US Army Corps of Engineers®

ISSUE DATE:		SOLICITATION NO.:		CONTRACT NO.:		SCALE:		AS SHOWN		MARK		DATE	

DESIGNED BY:

DRAWN BY:

CHECKED BY:

SUBMITTED BY:

SIZE: ISO A1

FILE NAME:

US ARMY CORPS OF ENGINEERS
JAPAN DISTRICT, OKINAWA AREA OFFICE
USAEJ-L UNIT 35132
APO, AP 96374-5132

SSFM
SSFM INTERNATIONAL, INC.
501 SUMNER STREET, SUITE 620
HONOLULU, HAWAII 96817


KADENA AIR BASE, OKINAWA, JAPAN
VEHICLE MAINTENANCE SHOP
FY20 MCA PN77833

PARTIAL SITE ELECTRICAL DEMOLITION PLAN 1 (CLIN 0001 - CLIN 0003)

SHEET ID

ES102

INTERMEDIATE DESIGN

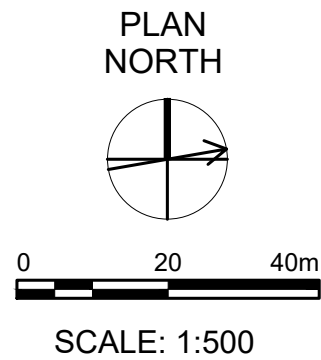

INTERMEDIATE DESIGN



1. SEE CIVIL AND TELECOMMUNICATIONS PLANS FOR SITE DEMOLITION WORK AND CLOSELY COORDINATE THE ELECTRICAL DEMOLITION WORK.
2. PRIOR TO ANY ELECTRICAL EQUIPMENT AND INFRASTRUCTURE DEMOLITION WORK, ENSURE THAT THE NEW EQUIPMENT AND INFRASTRUCTURE ARE ESTABLISHED TO MINIMIZE DISRUPTION TO THE OPERATIONS OF THE EXISTING FACILITIES.
3. THE CONTRACTOR SHALL BE RESPONSIBLE TO SUBMIT A PROPOSED PHASING SCHEME IN COORDINATION WITH CIVIL AND TELECOMMUNICATIONS WORK FOR REVIEW AND APPROVAL PRIOR TO START OF DEMOLITION WORK.

KEY NOTES

- 1 EXISTING CJP ,SET, DISTRIBUTION EQUIPMENT,AND ASSOCIATED FEEDERS SHALL REMAIN IN SERVICE.
- 2 EXISTING PRIMARY FEEDER SHALL BE REMAIN IN SERVICE.

CLIN 0001-0003

CLIN 0001:


- SITE PREPARATION WORK FOR VMS FACILITIES.
- LOONEY STREET AND ELECTRICAL INFRASTRUCTURE IMPROVEMENTS.
- RELOCATE CJP AND TRANSFORMER SERVING B871 (RECYCLING FACILITY) AND OTHER BUILDINGS.
- CONSTRUCTION OF VEHICLE MAINTENANCE SHOP, FIRE PUMP HOUSE, WATER STORAGE TANK, CABLE HUT, AND ASSOCIATED ELECTRICAL INFRASTRUCTURE.

CLIN 0002:

- CONSTRUCTION OF ORGANIZATIONAL EQUIPMENT STORAGE, POL STORAGE, AND ASSOCIATED ELECTRICAL INFRASTRUCTURE.

CLIN 0003:

- CONSTRUCTION OF ORGANIZATIONAL VEHICLE PARKING LOT AND SITE LIGHTING.
- CONSTRUCTION OF WASH RACK AND ASSOCIATED ELECTRICAL INFRASTRUCTURE.

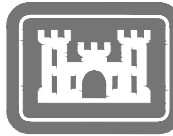

US Army Corps
of Engineers®

[illegible]

 SSPA INTERNATIONAL 507 SUMNER STREET, SUITE 620 HONOLULU, HAWAII 96817	DESIGNED BY:	ISSUE DATE:
	DRAWN BY:	SOLICITATION NO.:
	CHECKED BY:	CONTRACT NO.:
	SUBMITTED BY:	SCALE:
	SIZE:	AS SHOWN
	FILE NAME:	
	ISO A1	

KADENA AIR BASE, OKINAWA, JAPAN
VEHICLE MAINTENANCE SHOP
FY20 MCA PN77833

SHEET ID
ES104

INTERMEDIATE DESIGN



INTERMEDIATE DESIGN

INTERMEDIATE DESIGN

A — B — C — D — E — F — G — H — I — J — K — L — M — N — O — P




GENERAL NOTES

1. SEE CIVIL AND TELECOMMUNICATIONS PLANS FOR SITE DEMOLITION WORK AND CLOSELY COORDINATE THE ELECTRICAL DEMOLITION WORK.
2. PRIOR TO ANY ELECTRICAL EQUIPMENT AND INFRASTRUCTURE DEMOLITION WORK, ENSURE THAT THE NEW EQUIPMENT AND INFRASTRUCTURE ARE ESTABLISHED TO MINIMIZE DISRUPTION TO THE OPERATIONS OF THE EXISTING FACILITIES.
3. THE CONTRACTOR SHALL BE RESPONSIBLE TO SUBMIT A PROPOSED PHASING SCHEME IN COORDINATION WITH CIVIL AND TELECOMMUNICATIONS WORK FOR REVIEW AND APPROVAL PRIOR TO START OF DEMOLITION WORK.

KEY NOTES

- 1 REMOVE EXISTING SERVICE EQUIPMENT AND ASSOCIATED CIRCUITS BACK TO THE SOURCE. CONDUIT STUB OUT SHALL BE CUT BELOW GRADE AND CAPPED. EXISTING DUCTS SHALL BE ABANDONED IN PLACE.

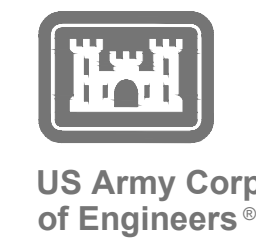[illegible]

DESIGNED BY: DRAWN BY: CHECKED BY: SUBMITTED BY:	ISSUE DATE: SOLICITATION NO.: CONTRACT NO.: SCALE: AS SHOWN	
	FILE NAME: ISO A1	501 SUNDRIEST, SUITE 620 HONOLULU, HAWAII 96817

KADENA AIR BASE, OKINAWA, JAPAN
VEHICLE MAINTENANCE SHOP
FY20 MCA PN17833

SHEET ID
ES14


INTERMEDIATE DESIGN

CLIN 0004


CLIN 0004

- CONSTRUCTION OF TEMPORARY FACILITIES AT SWING SPACE SITE MUST BE COMPLETED PRIOR TO DEMOLITION OF EXISTING ADA BUILDINGS (B4040 THRU B4047) AND SITE PREPARATION WORK FOR SSA FACILITIES.
- CONSTRUCTION OF NEW SUPPLY SUPPORT ACTIVITY (SSA) WAREHOUSE, STORAGE SHED AND ASSOCIATED ELECTRICAL INFRASTRUCTURE.
- CONSTRUCTION OF SSA PARKING LOT AND SITE LIGHTING.

P
O
N
M
L
K
J
I
H
G
F
E
D
C
B
A

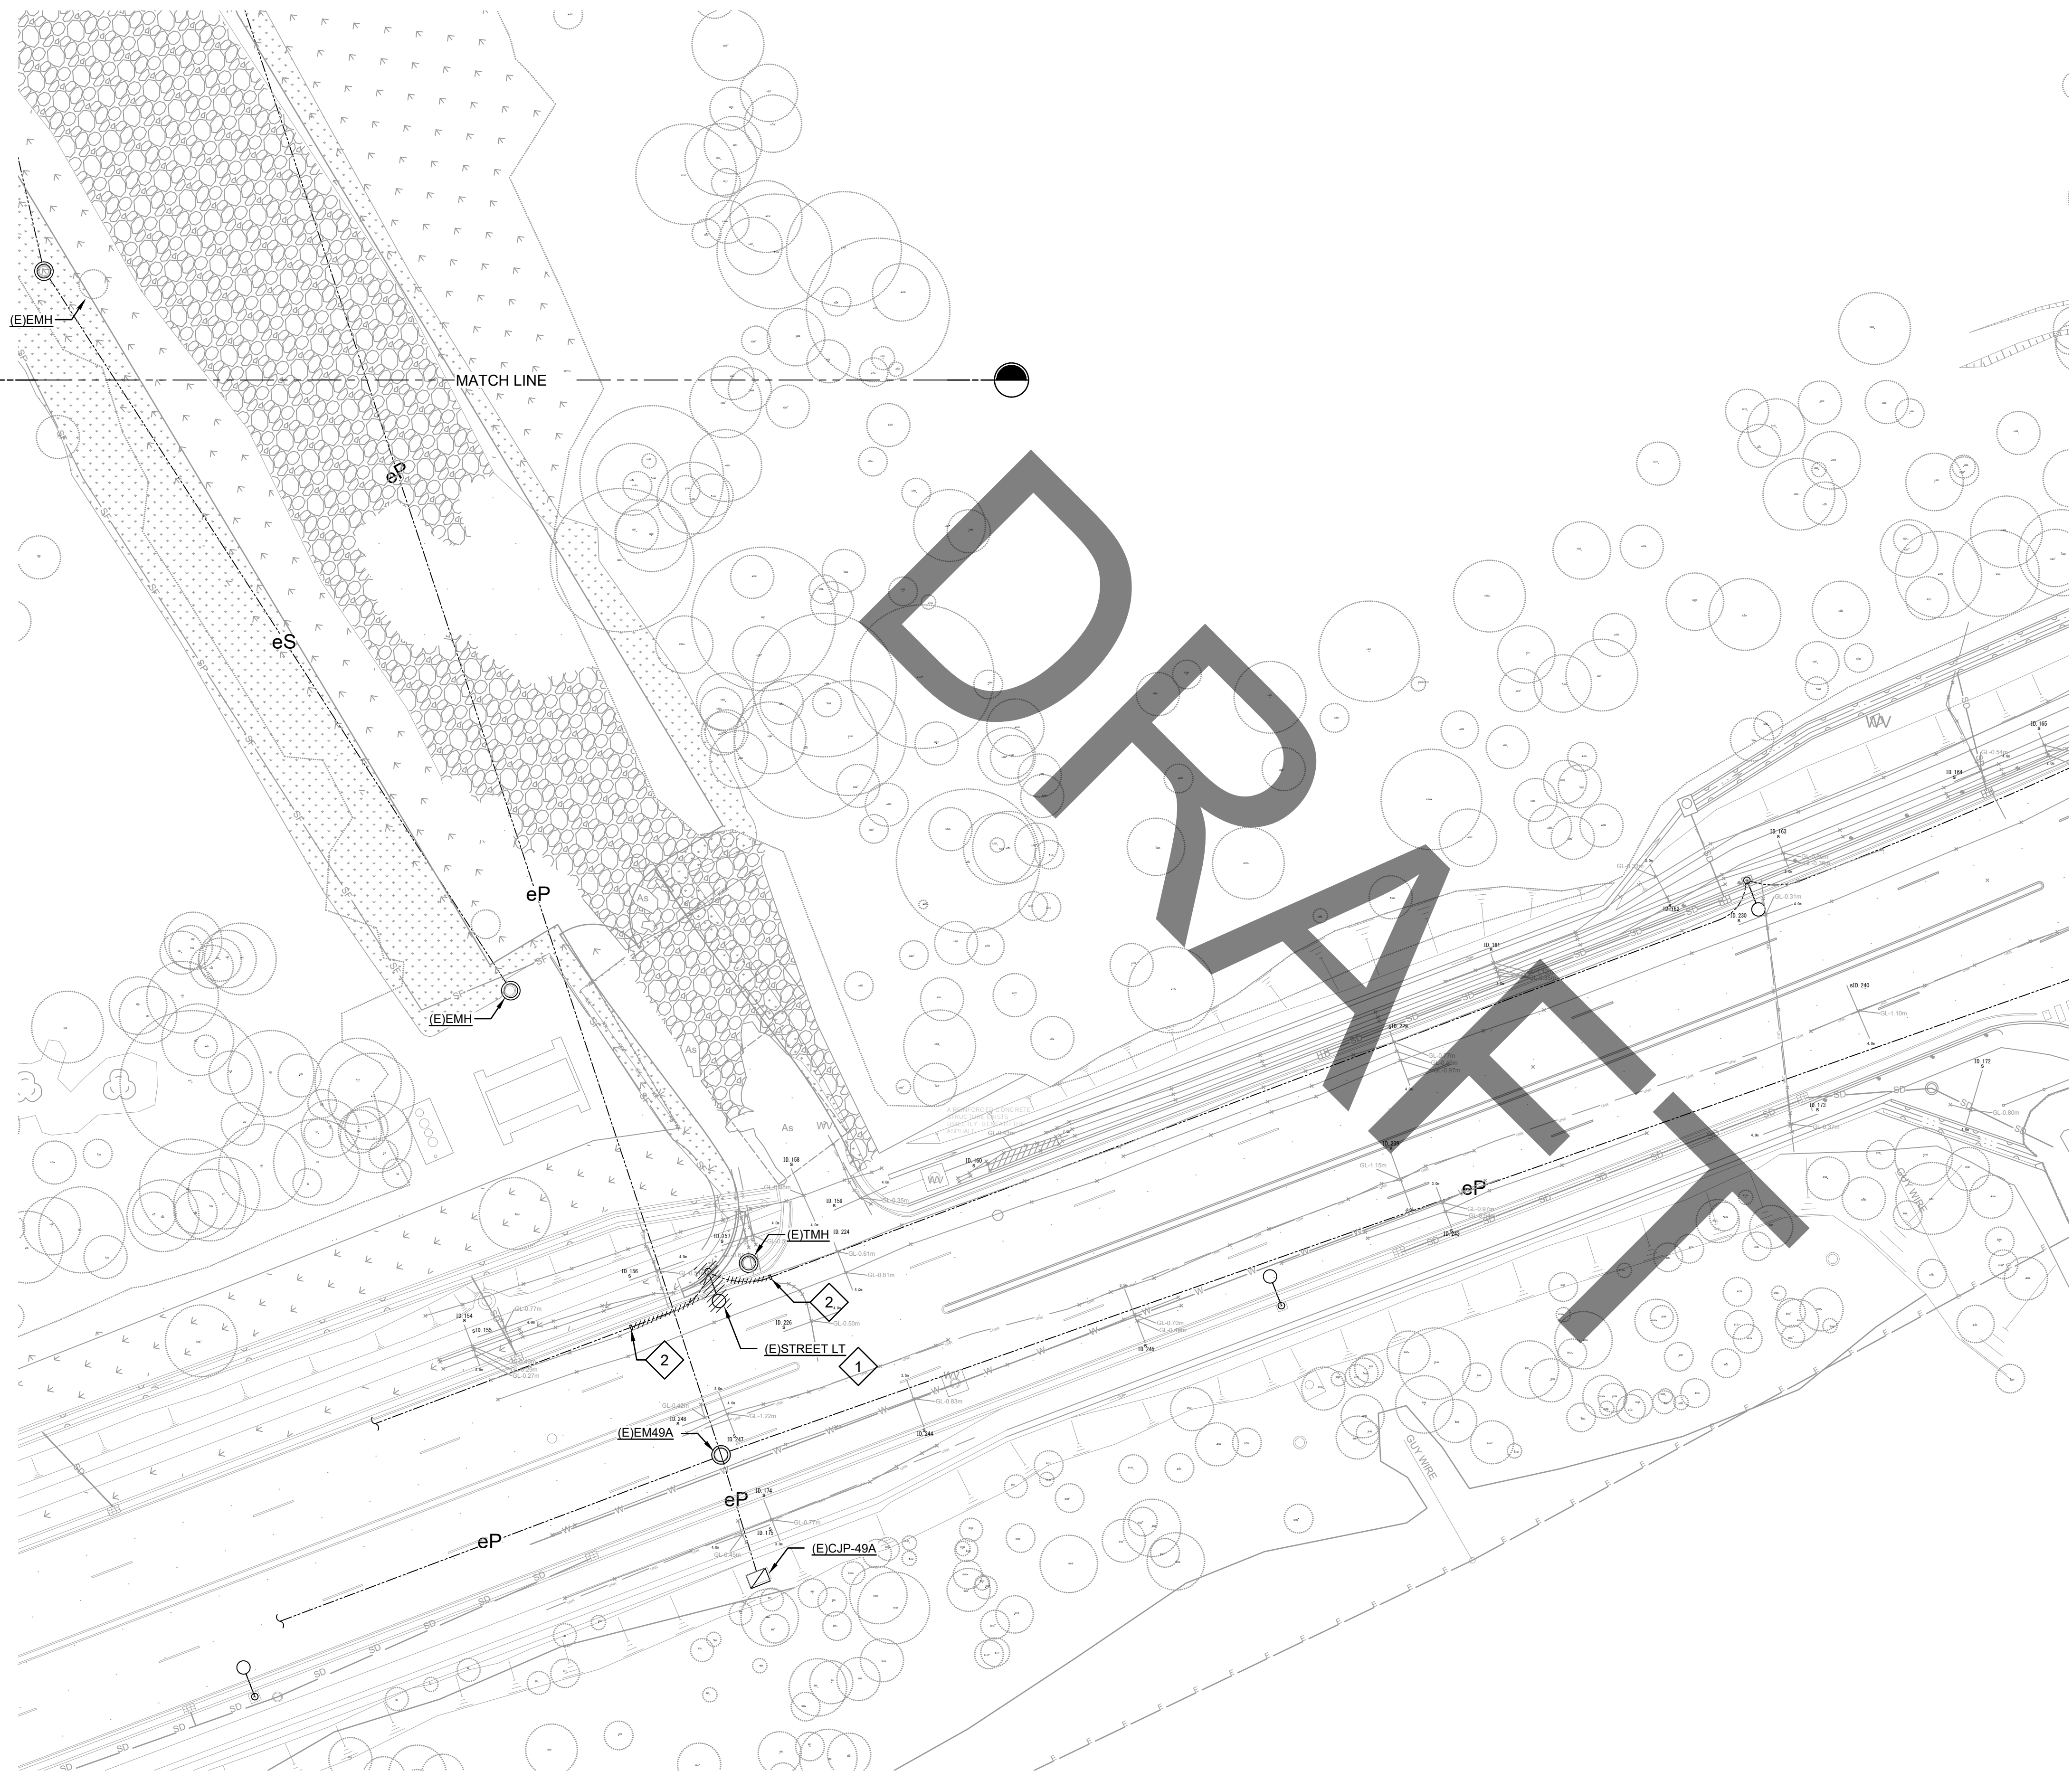

A1 PARTIAL SITE ELECTRICAL DEMOLITION PLAN 2 - COF SS (CLIN0004)

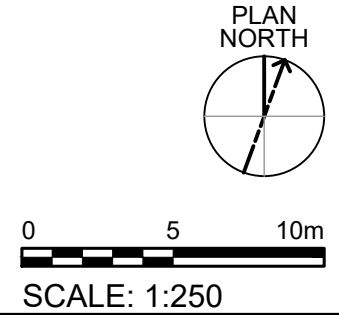

GENERAL NOTES

1. SEE CIVIL AND TELECOMMUNICATIONS PLANS FOR SITE DEMOLITION WORK AND CLOSELY COORDINATE THE ELECTRICAL DEMOLITION WORK.
2. PRIOR TO ANY ELECTRICAL EQUIPMENT AND INFRASTRUCTURE DEMOLITION WORK, ENSURE THAT THE NEW EQUIPMENT AND INFRASTRUCTURE ARE ESTABLISHED TO MINIMIZE DISRUPTION TO THE OPERATIONS OF THE EXISTING FACILITIES.
3. THE CONTRACTOR SHALL BE RESPONSIBLE TO SUBMIT A PROPOSED PHASING SCHEME IN COORDINATION WITH CIVIL AND TELECOMMUNICATIONS WORK FOR REVIEW AND APPROVAL PRIOR TO START OF DEMOLITION WORK.

KEY NOTES

- 1 EXISTING STREET LIGHT SHALL BE REMOVED AND RELOCATED.
- 2 EXISTING STREET LIGHT CIRCUIT SHALL BE CUT AND REMOVED BACK TO THE NEXT STREET LIGHT POLE. INTERCEPT EXISTING DUCT AND RE-ROUTE TO THE RELOCATED POLE. PROVIDE NEW NEW CIRCUIT TO RESTORE THE OPERATION.

CLIN 0004

- CLIN 0004**
- CONSTRUCTINO OF TEMPORARY FACILITIES AT SWING SPACE SITE MUST BE COMPLETED PRIOR TO DEMOLITION OF EXISTING ADA BUILDINGS (B4040 THRU B4047) AND SITE PREPARATION WORK FOR SSA FACILITIES.
 - CONSTRUCTION OF NEW SUPPLY SUPPORT ACTIVITY (SSA) WAREHOUSE, STORAGE SHED AND ASSOCIATED ELECTRICAL INFRASTRUCTURE.
 - CONSTRUCTION OF SSA PARKING LOT AND SITE LIGHTING.

US Army Corps
of Engineers®

ISSUE DATE:		SOLICITATION NO.:		CONTRACT NO.:		SCALE:		AS SHOWN		FILE NAME:	
DESIGNED BY:		DRAWN BY:		CHECKED BY:		SUBMITTED BY:		SIZE:		ISO A1	

US ARMY CORPS OF ENGINEERS
JAPAN DISTRICT, OKINAWA AREA OFFICE
USAED-J UNIT 35132
APO, AP 96374-5132

SSFM
SSFM INTERNATIONAL, INC.
501 SUMNER STREET, SUITE 620
HONOLULU, HAWAII 96817

KADENA AIR BASE, OKINAWA, JAPAN
VEHICLE MAINTENANCE SHOP
FY20 MCA PN77833


PARTIAL SITE ELECTRICAL DEMOLITION PLAN 2 - COF SS (CLIN 0004)

SHEET ID

ES143

INTERMEDIATE DESIGN

A — B — C — D — E — F — G — H — I — J — K — L — M — N — O — P —

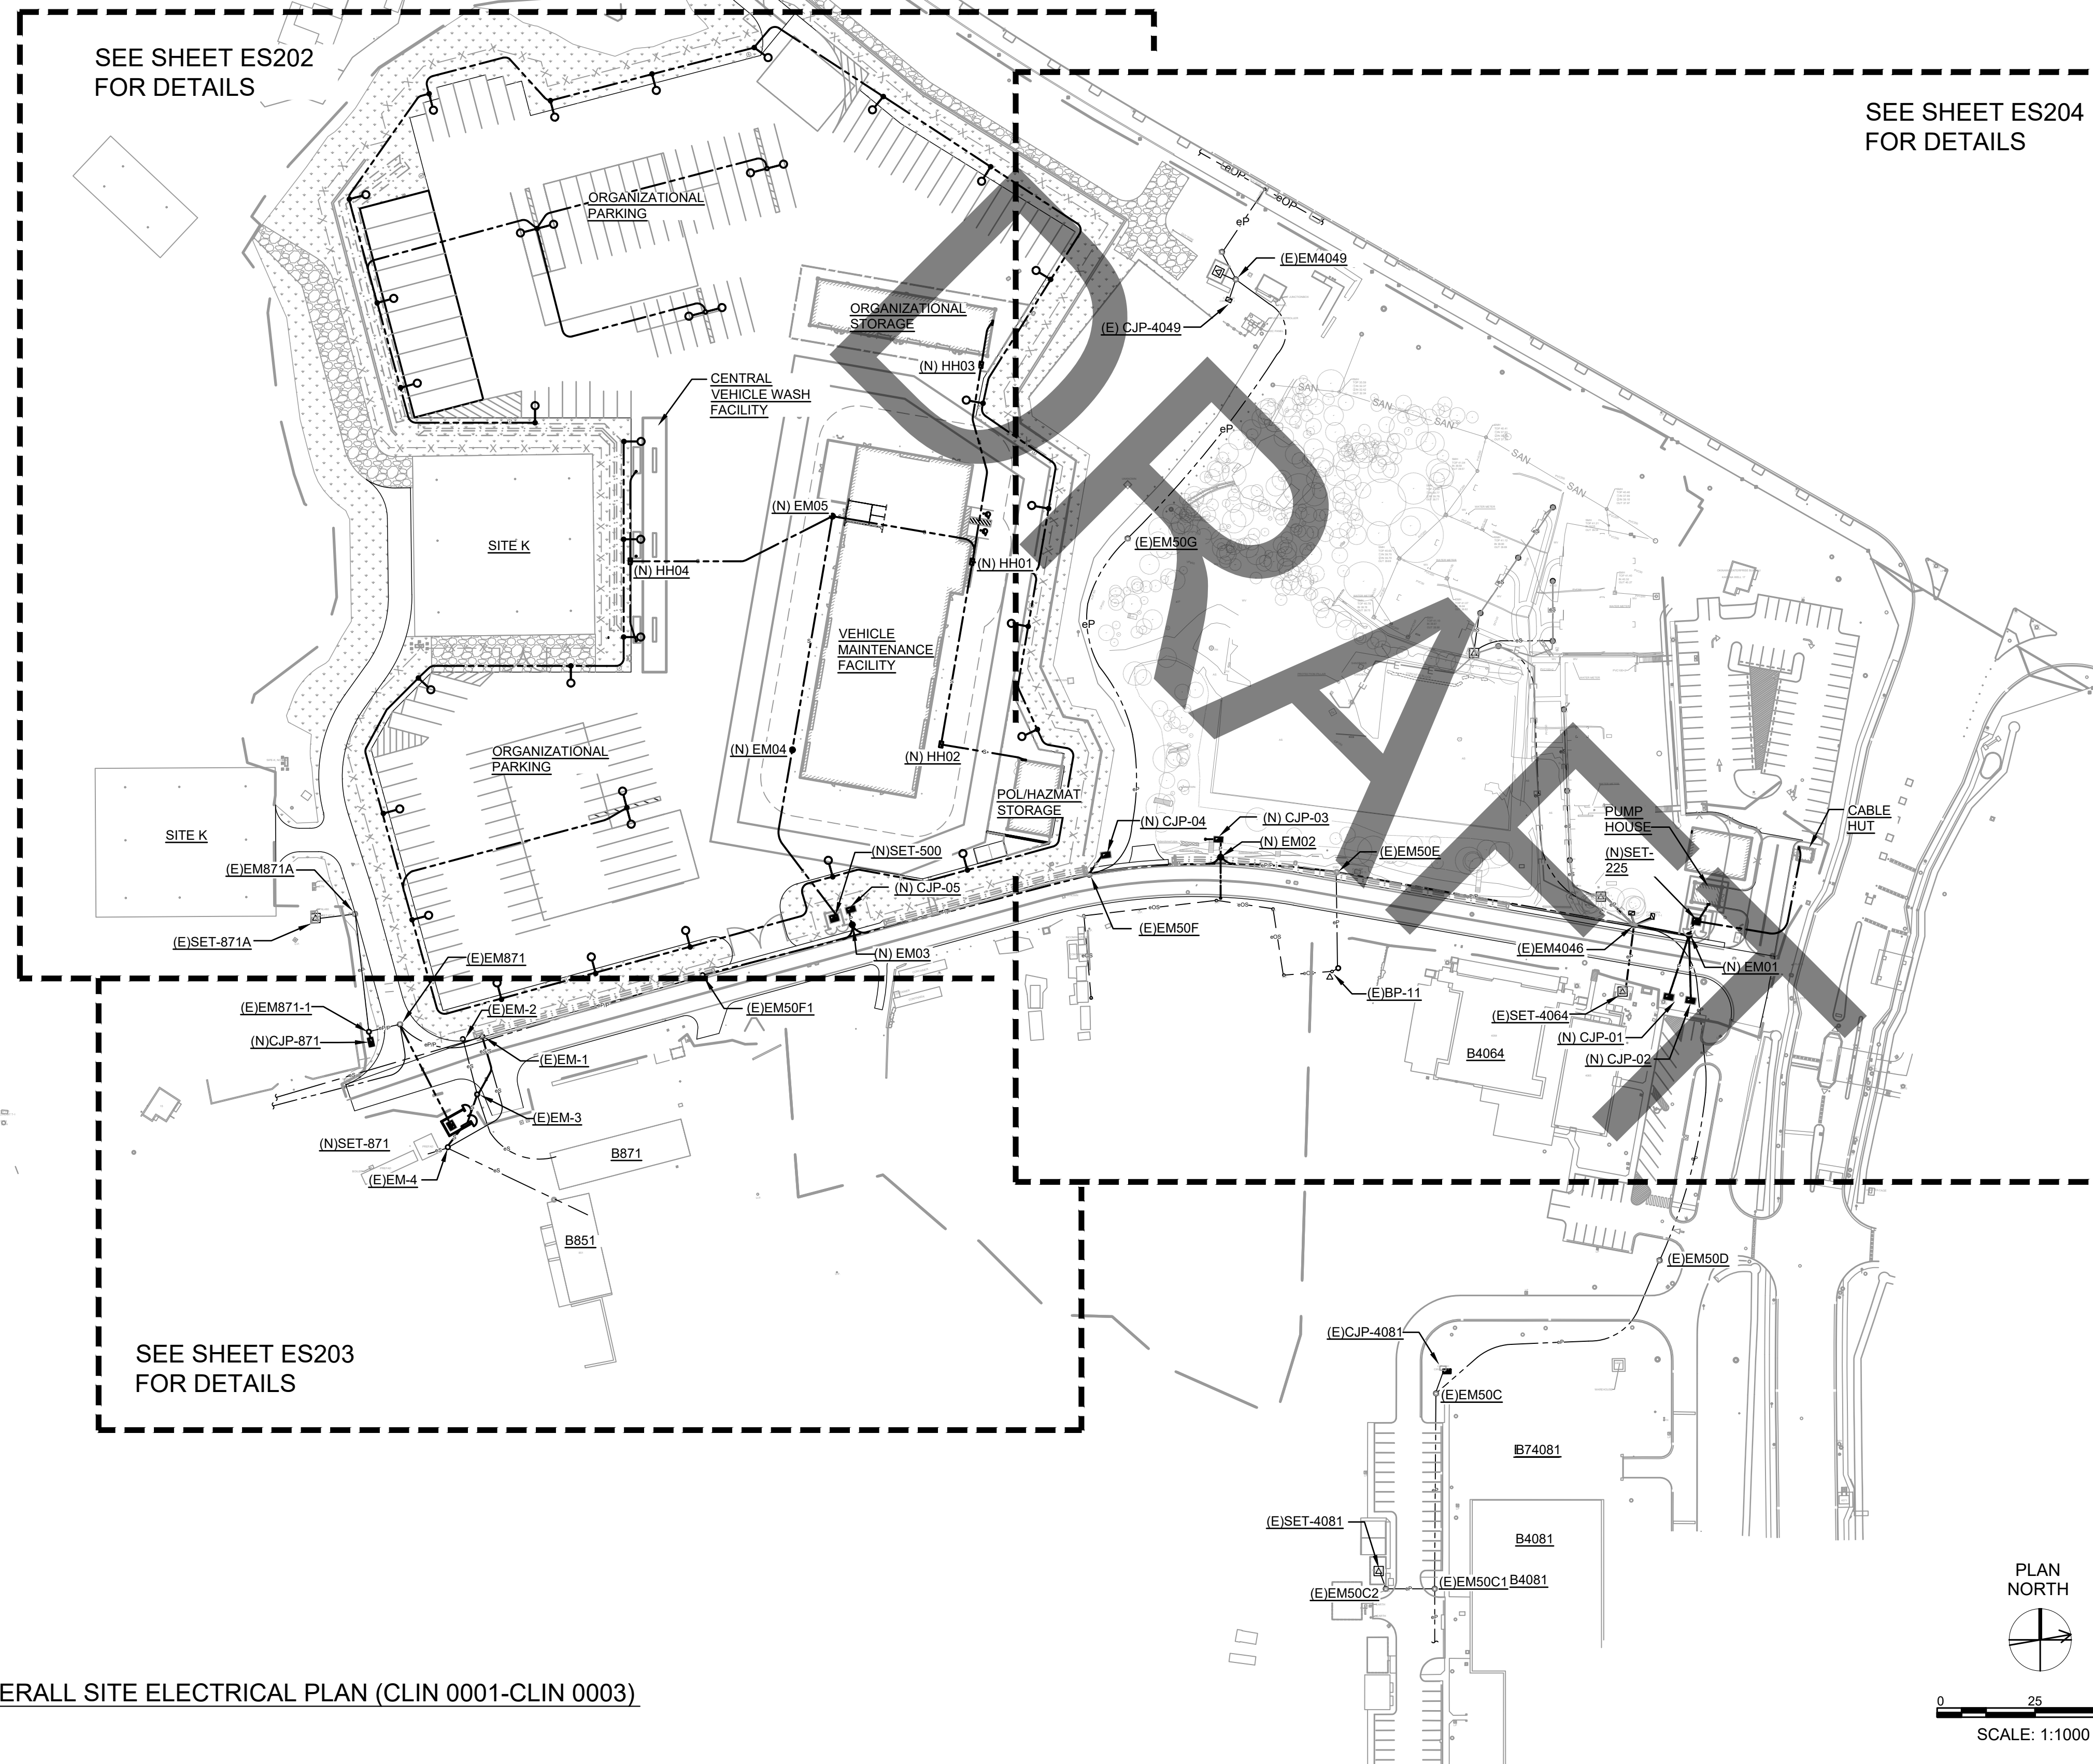

GENERAL NOTES

1. SEE CIVIL PLANS FOR CIVIL SITE DEMOLITION WORK AND CLOSELY COORDINATE THE ELECTRICAL DEMOLITION WORK.
2. PRIOR TO ANY ELECTRICAL EQUIPMENT AND INFRASTRUCTURE DEMOLITION WORK, ENSURE THAT THE NEW EQUIPMENT AND INFRASTRUCTURE ARE ESTABLISHED TO MINIMIZE DISRUPTION TO THE OPERATIONS OF THE EXISTING FACILITIES.
3. THE CONTRACTOR SHALL BE RESPONSIBLE TO SUBMIT A PROPOSED PHASING SCHEME FOR REVIEW AND APPROVAL PRIOR TO START OF DEMOLITION WORK.



**U.S. Army Corps
Engineers®**

KEY NOTES

[illegible]

US ARMY CORPS OF ENGINEERS JAPAN DISTRICT, OKINAWA AREA OFFICE USAEJL UNIT 35132 APO SF 96374-1532		ORDER DATE: ORDERED BY: DRAWN BY: CHECKED BY: SUBMITTED BY: FILE NAME:
		SOLICITATION NO.: CONTRACT NO.: SCALE: AS SHOWN
Ssfm INTERNATIONAL, INC. 501 SUMNER STREET, SUITE 620 HONOLULU, HAWAII 96817		SIZE: ISO A1


KADENA AIR BASE, OKINAWA, JAPAN
VEHICLE MAINTENANCE SHOP
FY20 MCA PN77833

SHEET ID

ES201

INTERMEDIATE DESIGN

P
O
N
M
L
K
J
I
H
G
F
E
D
C
B
A

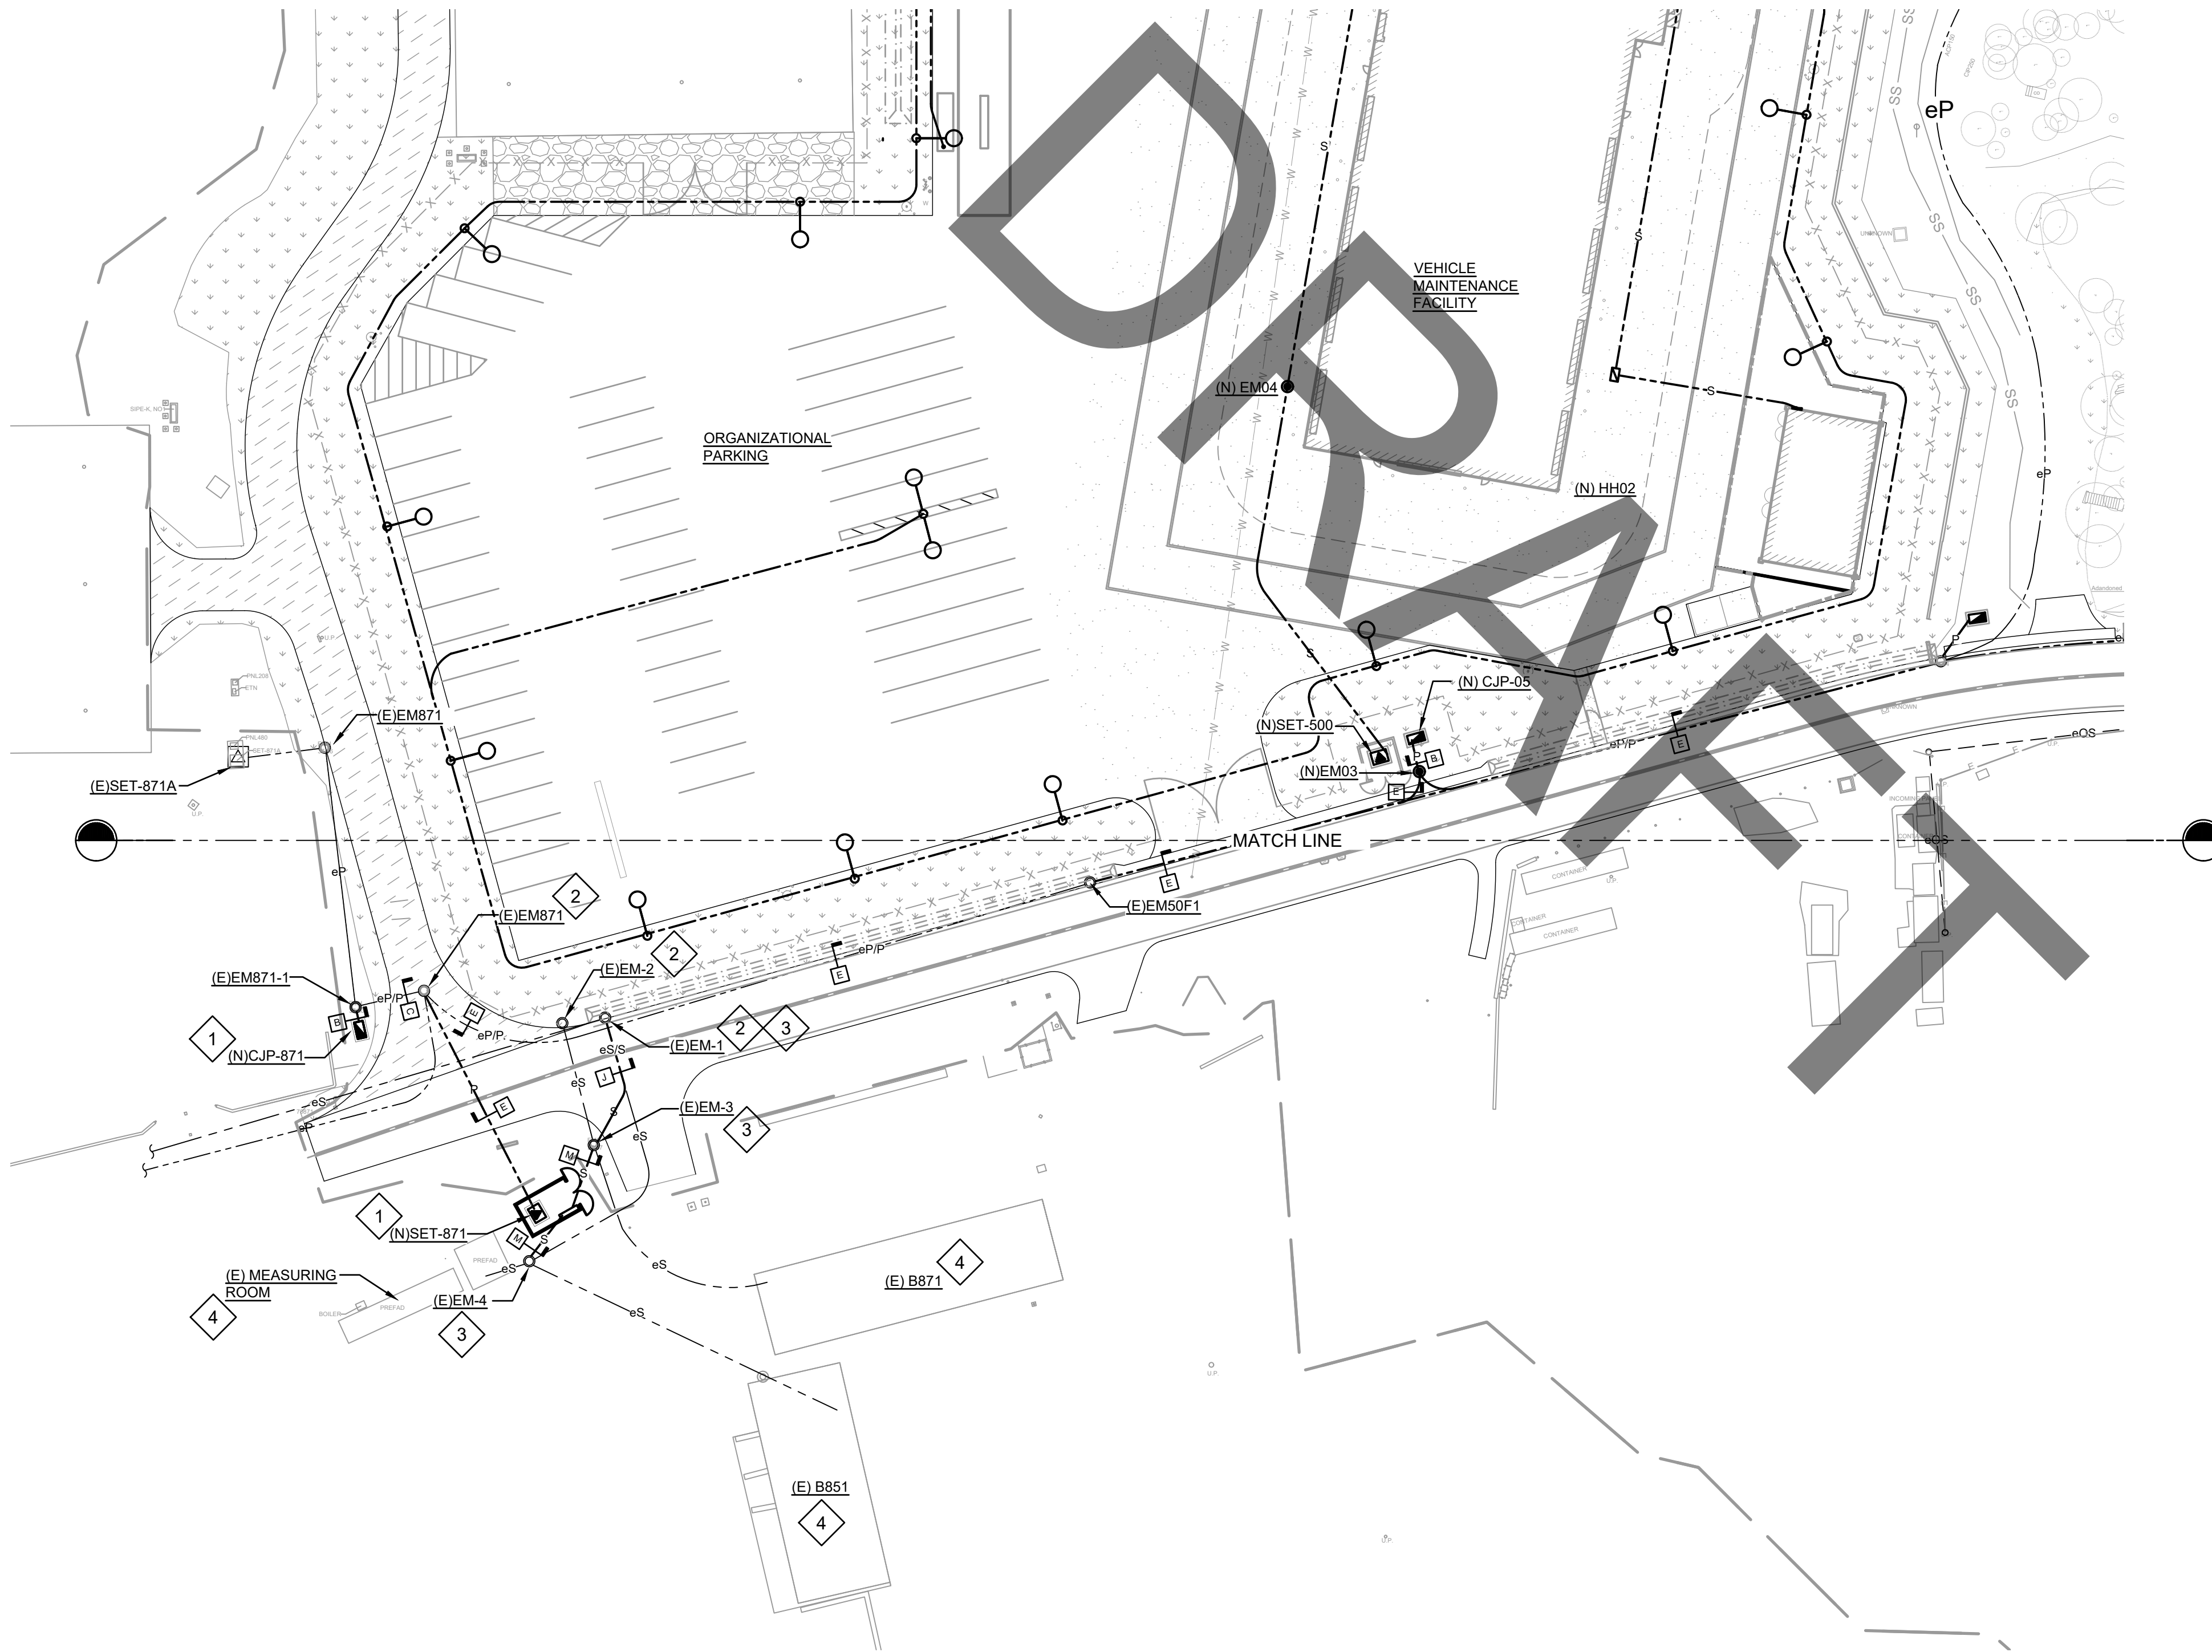

(A1) PARTIAL SITE ELECTRICAL PLAN -2 (CLIN 0001-CLIN 0003)


1:500



SCALE: 1:500

GENERAL NOTES

1. ALL DIMENSIONS SHOWN IN CALLOUT/NOTES ARE IN METERS UNLESS OTHERWISE NOTED.

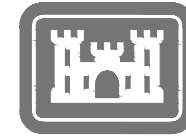

US Army Corps
of Engineers®

KEY NOTES

- 1 PROVIDE NEW CJP-871, SET-871, DISTRIBUTION EQUIPMENT, AND ASSOCIATED PRIMARY AND SECONDARY INFRASTRUCTURE PRIOR TO DEMOLITION OF THE EXISTING.
- 2 EXISTING MANHOLES SHALL BE SALVAGED AND REUSED. MODIFY MANHOLE FINISH TO MATCH THE FINAL GRADING.
- 3 PROVIDE NEW SECONDARY FEEDERS AND INTERCEPT EXISTING TO COMPLETE THE SWITCHOVER.
- 4 UPON CONFIRMING THAT ALL THE BUILDING SERVICES ARE RESTORED OFF THE NEW TRANSFORMER AND DISTRIBUTION SYSTEM, DEMOLISH EXISTING CJP-871, SET-871 AND DISTRIBUTION EQUIPMENT TO FACILITATE CONSTRUCTION OF NEW PARKING LOT AND ACCESS ROAD.

CLIN 0001-0003

- CLIN 0001:**
- SITE PREPARATION WORK FOR VMS FACILITIES.
 - LOONEY STREET AND ELECTRICAL INFRASTRUCTURE IMPROVEMENTS.
 - RELOCATE CJP AND TRANSFORMER SERVING B871 (RECYCLING FACILITY) AND OTHER BUILDINGS.
 - CONSTRUCTION OF VEHICLE MAINTENANCE SHOP, FIRE PUMP HOUSE, WATER STORAGE TANK, CABLE HUT, AND ASSOCIATED ELECTRICAL INFRASTRUCTURE.
- CLIN 0002:**
- CONSTRUCTION OF ORGANIZATIONAL EQUIPMENT STORAGE, POL STORAGE, AND ASSOCIATED ELECTRICAL INFRASTRUCTURE.
- CLIN 0003:**
- CONSTRUCTION OF ORGANIZATIONAL VEHICLE PARKING LOT AND SITE LIGHTING.
 - CONSTRUCTION OF WASH RACK AND ASSOCIATED ELECTRICAL INFRASTRUCTURE.

ISSUE DATE:
DESIGNED BY:
DRAWN BY:
CHECKED BY:
SUBMITTED BY:
SIZE: ISO A1
FILE NAME:


US ARMY CORPS OF ENGINEERS
JAPAN DISTRICT, OKINAWA AREA OFFICE
USAED-J UNIT 35132
APO, AP 96374-5132
SSFM
SSFM INTERNATIONAL, INC.
501 SUMNER STREET, SUITE 620
HONOLULU, HAWAII 96817

KADENA AIR BASE, OKINAWA, JAPAN
VEHICLE MAINTENANCE SHOP
FY20 MCA PN77833
PARTIAL SITE ELECTRICAL PLAN 2 (CLIN 0001 - CLIN 0003)


SHEET ID

ES203

INTERMEDIATE DESIGN

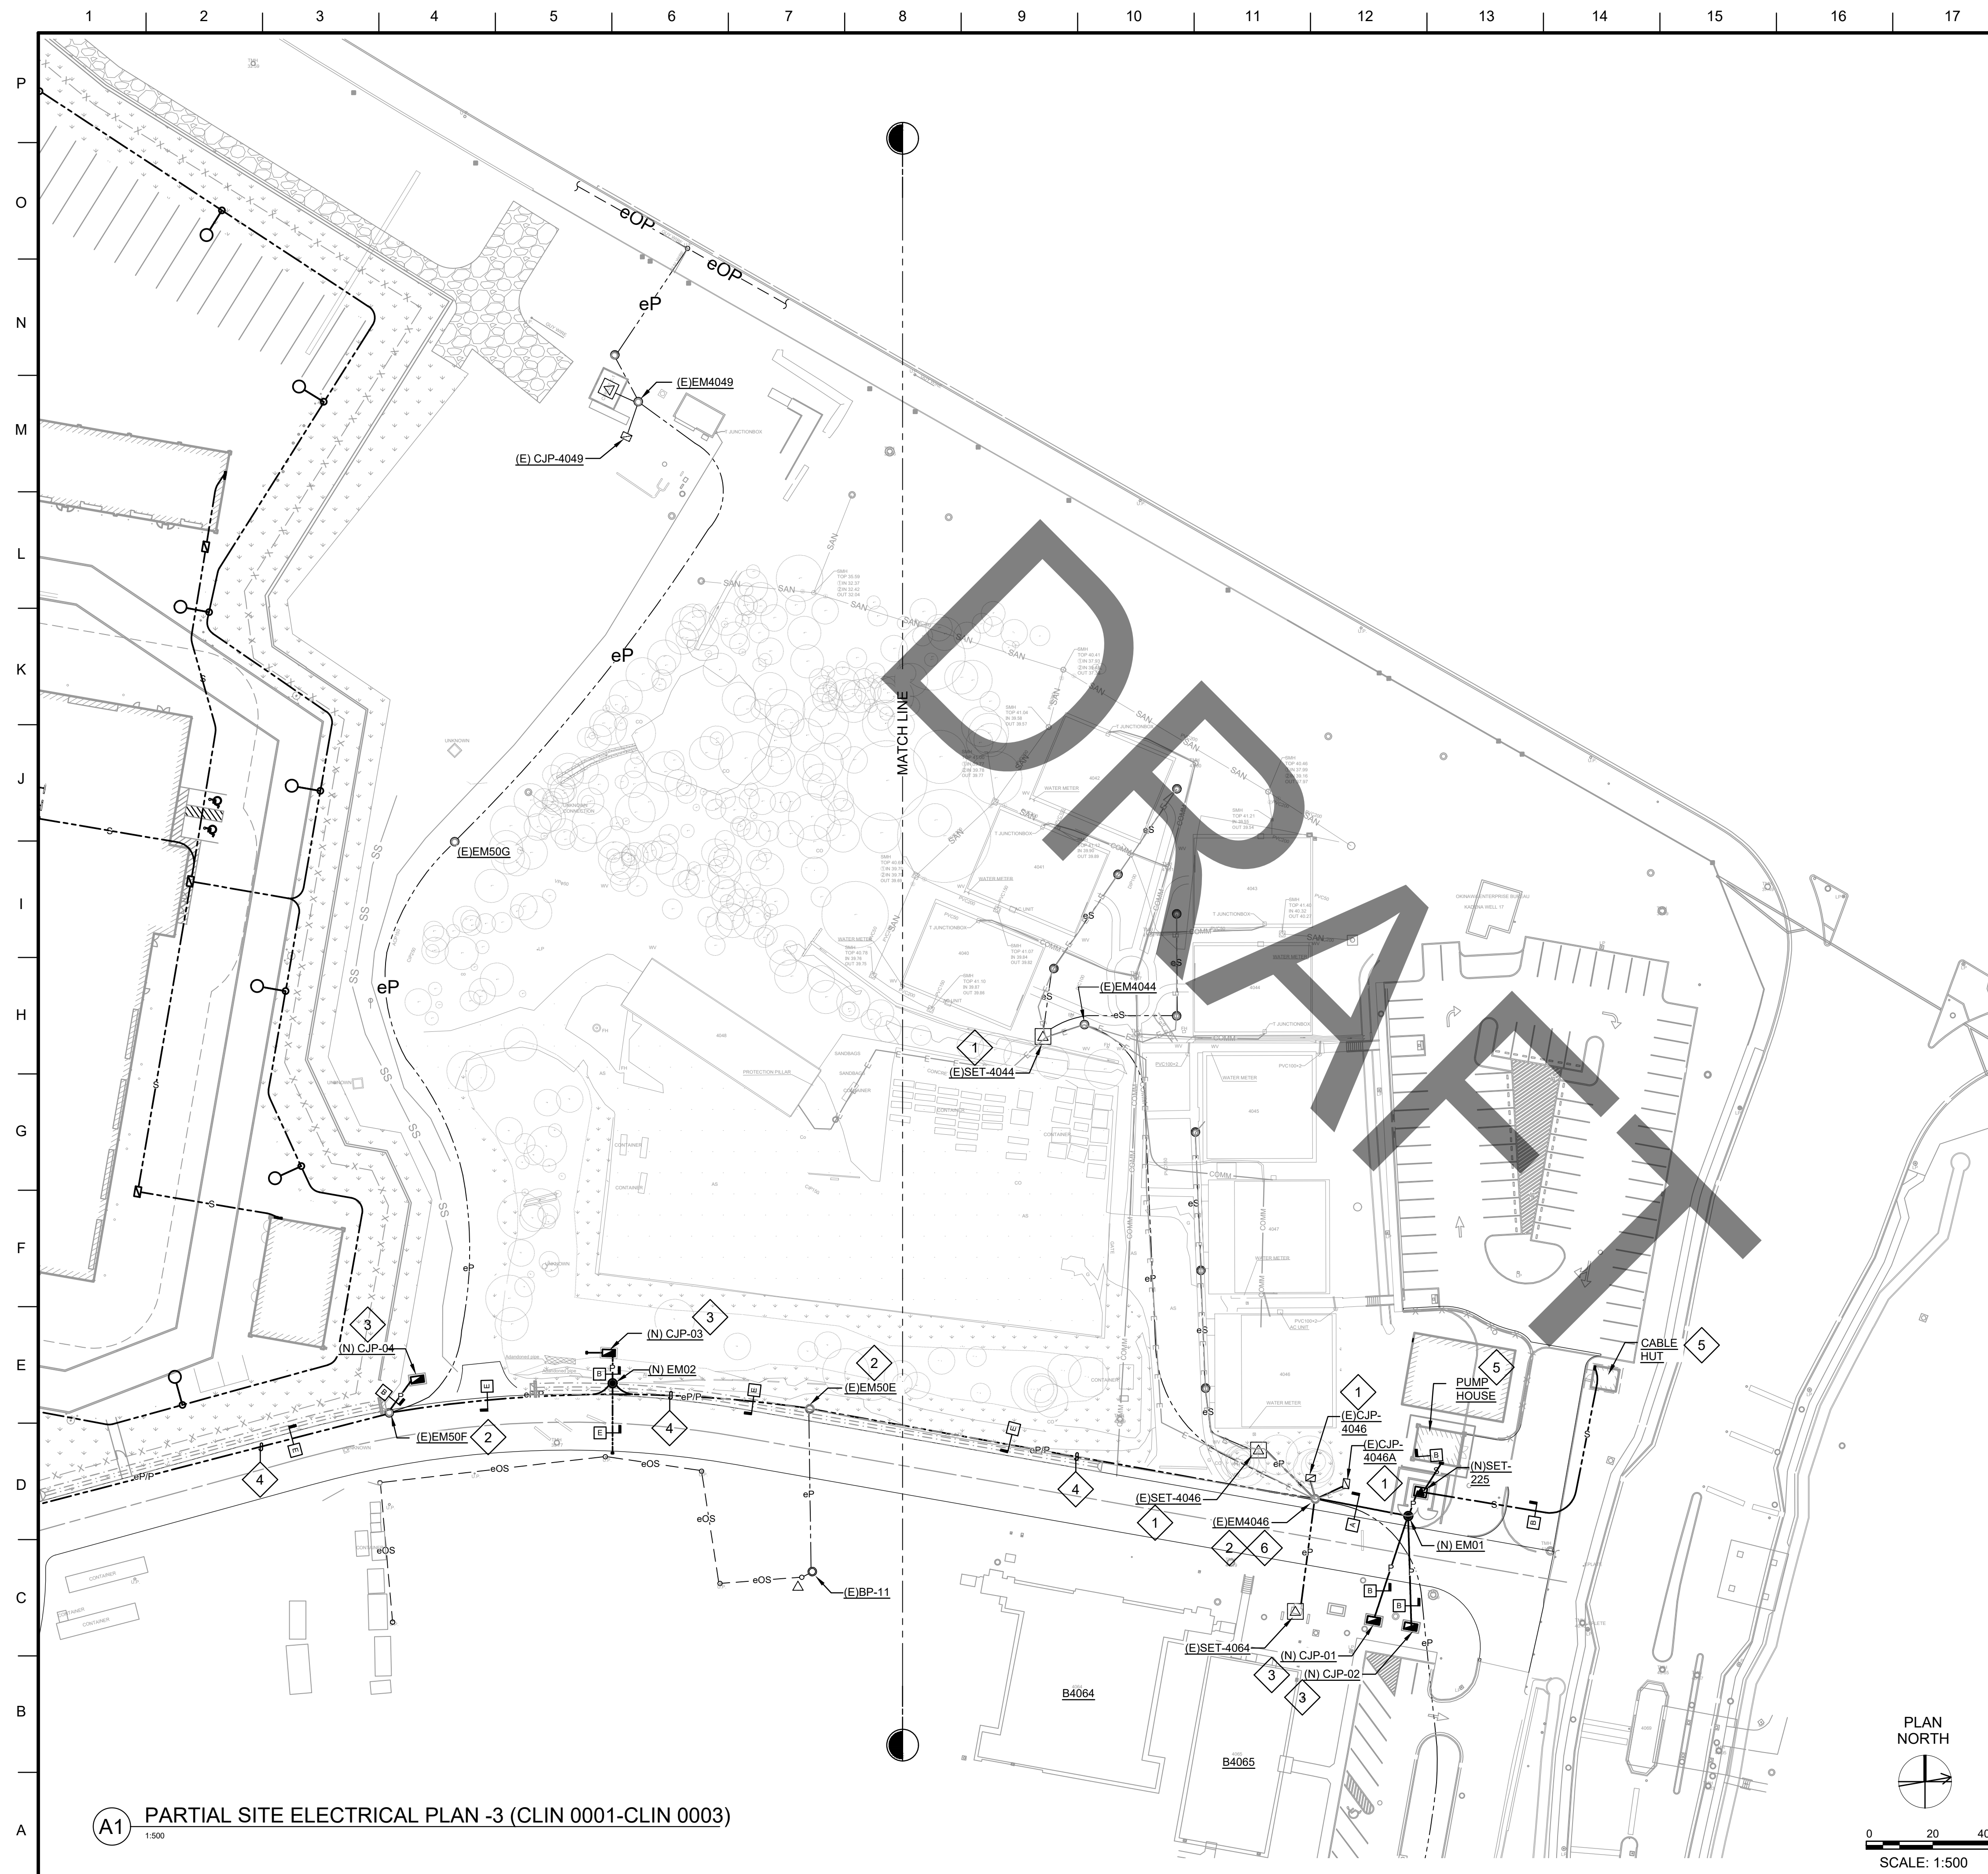

INTERMEDIATE DESIGN

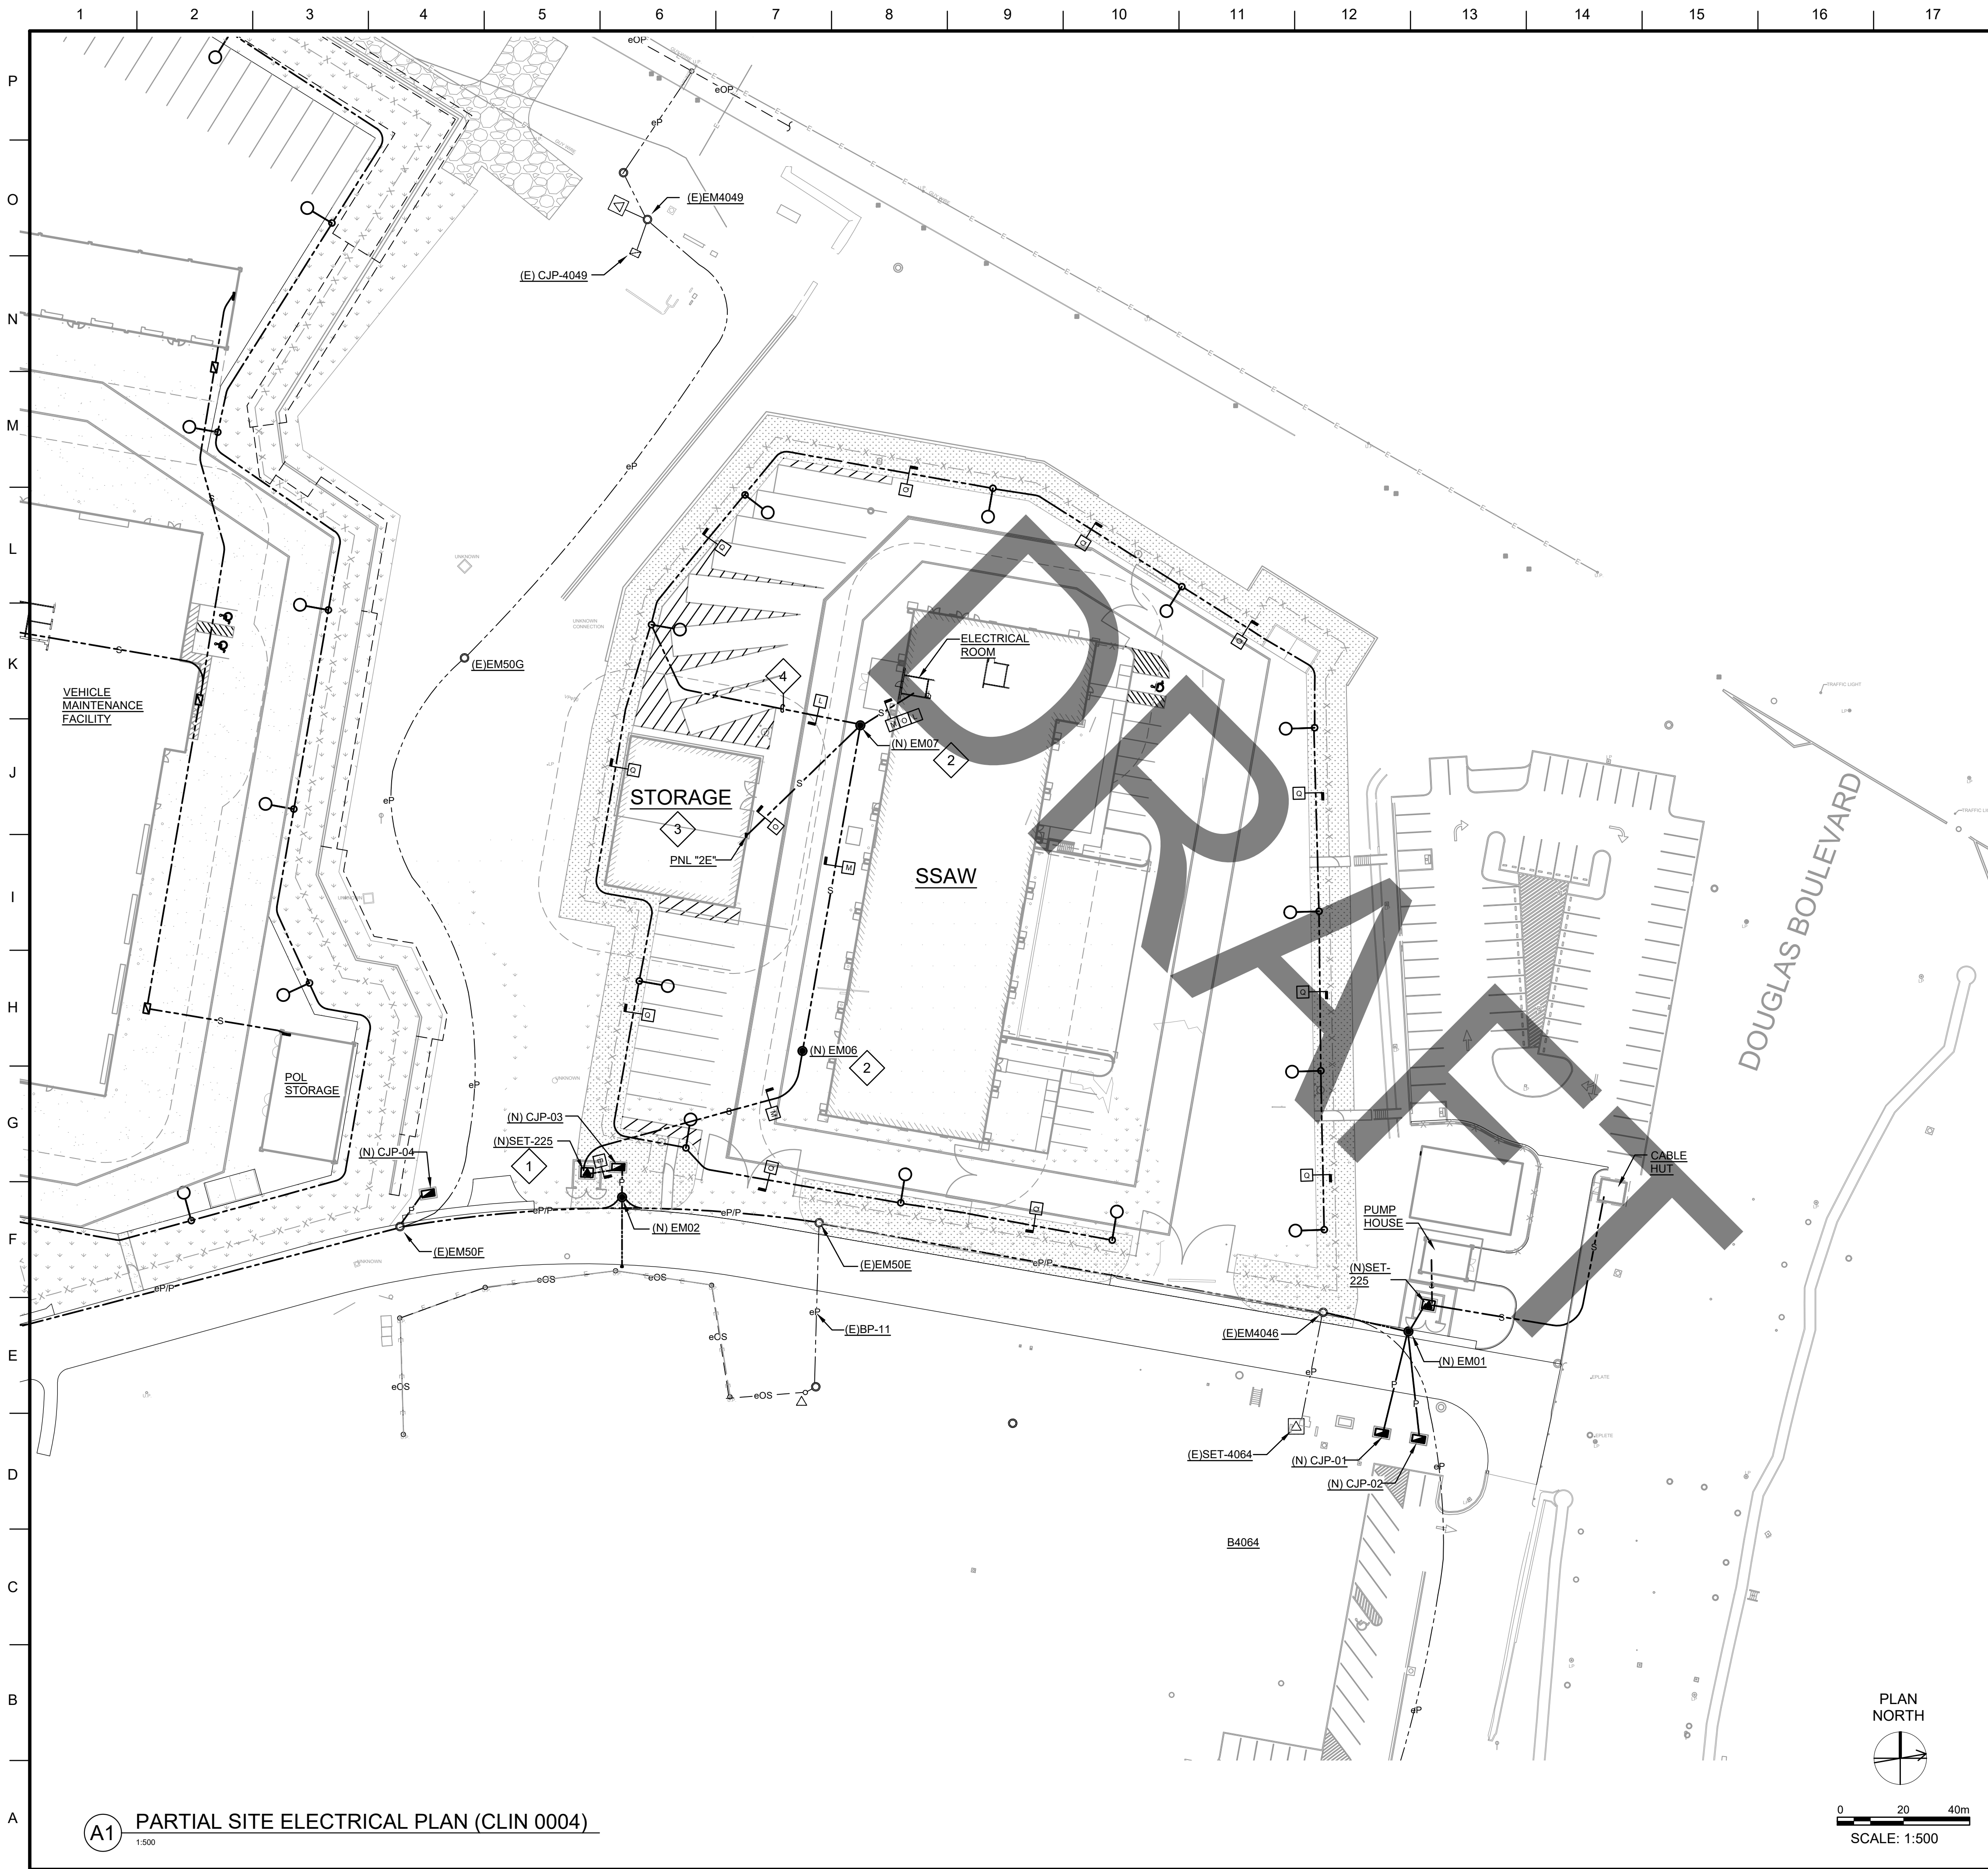

(A1) PARTIAL SITE ELECTRICAL PLAN (CLIN 0004)

GENERAL NOTES

1. SEE CIVIL PLANS FOR CIVIL SITE DEMOLITION WORK AND CLOSELY COORDINATE THE ELECTRICAL DEMOLITION WORK.
2. PRIOR TO ANY ELECTRICAL EQUIPMENT AND INFRASTRUCTURE DEMOLITION WORK, ENSURE THAT THE NEW EQUIPMENT AND INFRASTRUCTURE ARE ESTABLISHED TO MINIMIZE DISRUPTION TO THE OPERATIONS OF THE EXISTING FACILITIES.
3. THE CONTRACTOR SHALL BE RESPONSIBLE TO SUBMIT A PROPOSED PHASING SCHEME FOR REVIEW AND APPROVAL PRIOR TO START OF DEMOLITION WORK.

KEY NOTES

1. EXTEND DUCT FROM CJP-03 TO NEW TRANSFORMER (SET-225) AND COMPLETE THE PRIMARY FEEDER INSTALLATION.
2. PROVIDE SECONDARY FEEDER INFRASTRUCTURE AND SERVICE CONDUCTORS TO SSAW FROM TRANSFORMER (SET-225).
3. PROVIDE ELECTRICAL SERVICE TO STORAGE SHED FROM SSAW BUILDING.
4. PROVIDE SSA PARKING LOT AND SITE PERIMETER LIGHTING.

CLIN 0004

- CLIN 0004**
- CONSTRUCTINO OF TEMPORARY FACILITIES AT SWING SPACE SITE MUST BE COMPLETED PRIOR TO DEMOLITION OF EXISTING ADA BUILDINGS (B4040 THRU B4047) AND SITE PREPARATION WORK FOR SSA FACILITIES.
 - CONSTRUCTION OF NEW SUPPLY SUPPORT ACTIVITY (SSA) WAREHOUSE, STORAGE SHED AND ASSOCIATED ELECTRICAL INFRASTRUCTURE.
 - CONSTRUCTION OF SSA PARKING LOT AND SITE LIGHTING.

US Army Corps of Engineers®

ISSUE DATE:		DESIGNED BY:		JAPAN DISTRICT, OKINAWA AREA OFFICE	
		DRAWN BY:		USAED-J UNIT 35132	
		CHECKED BY:		APO, AP 96374-5132	
		SUBMITTED BY:		SSFM INTERNATIONAL, INC.	
		SIZE:		501 SUMNER STREET, SUITE 620	
		FILE NAME:		HONOLULU, HAWAII 96817	

KADENA AIR BASE, OKINAWA, JAPAN

VEHICLE MAINTENANCE SHOP

FY20 MCA PN77833


PARTIAL SITE ELECTRICAL PLAN (CLIN 0004)

SHEET ID


ES232

INTERMEDIATE DESIGN

SEE SHEET ES242
FOR DETAILS

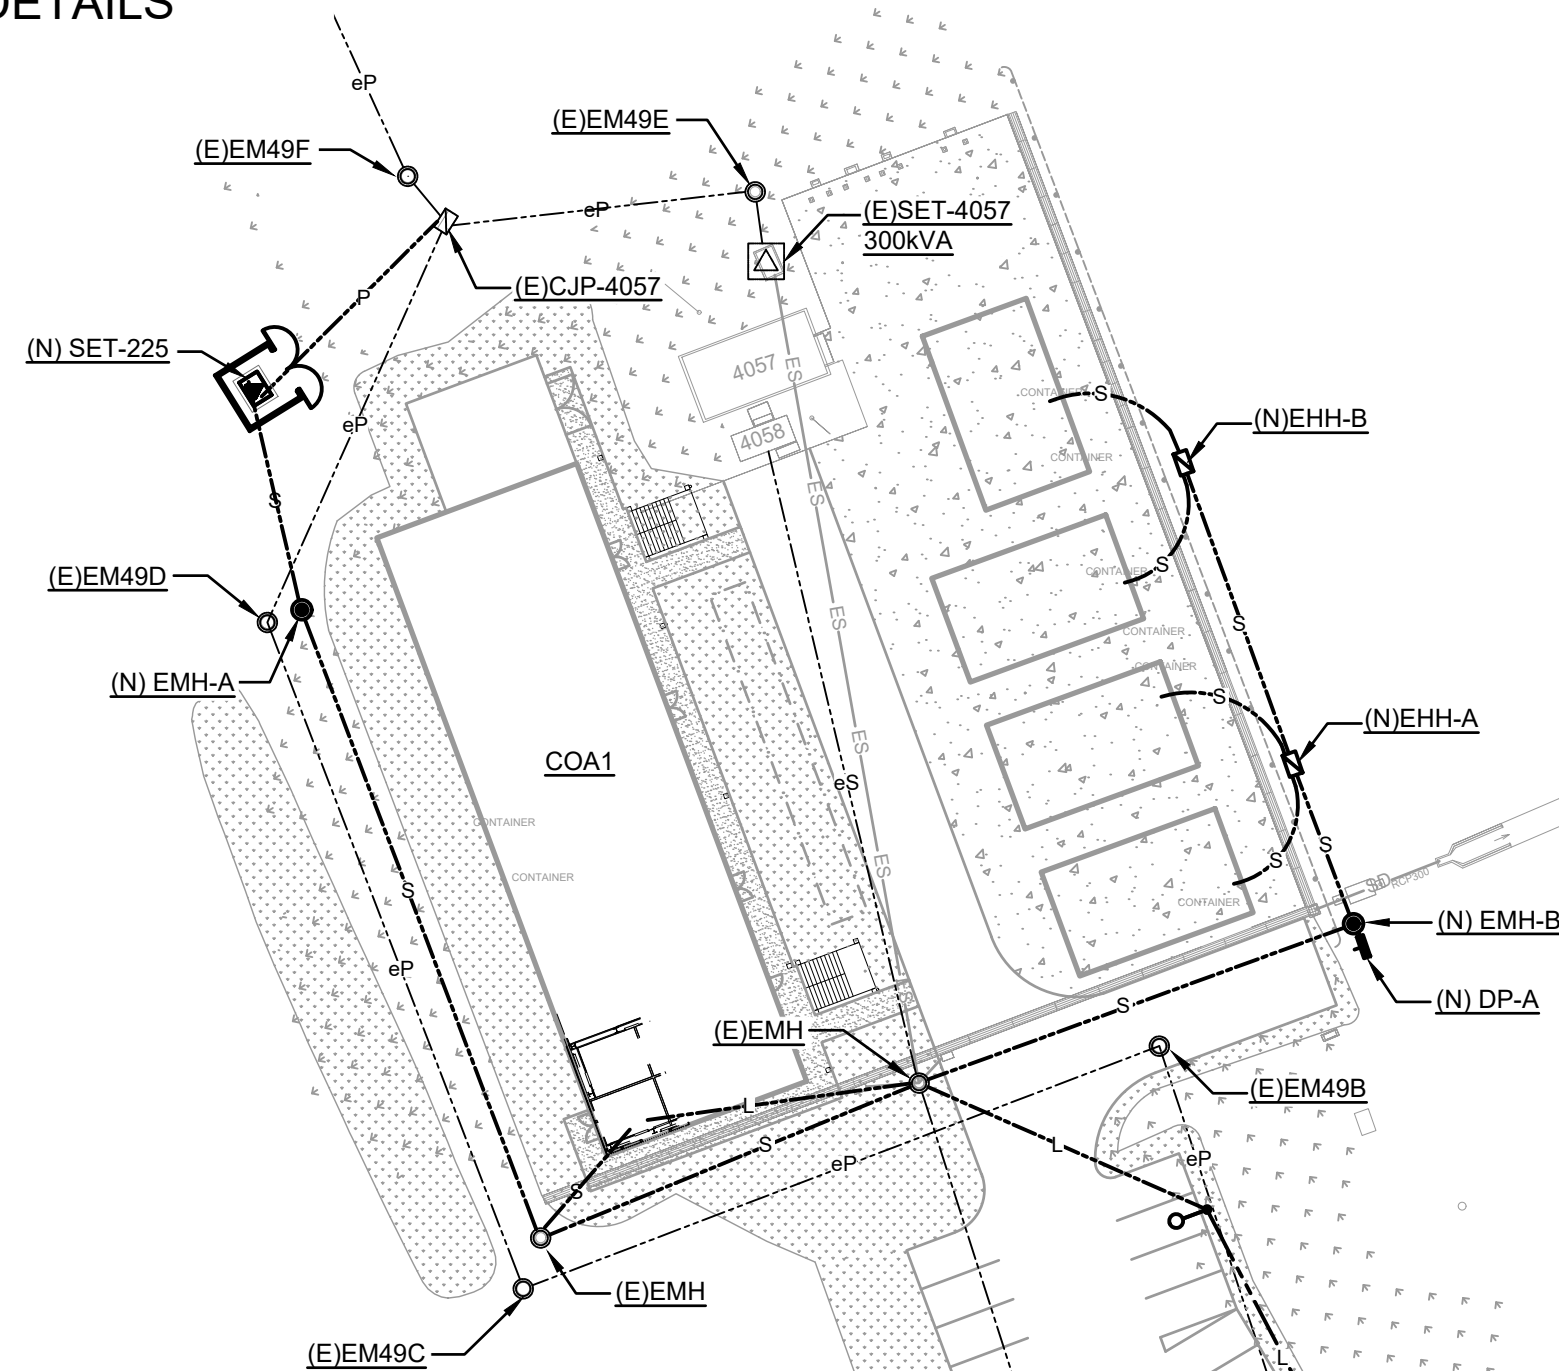

SEE SHEET ES243
FOR DETAILS

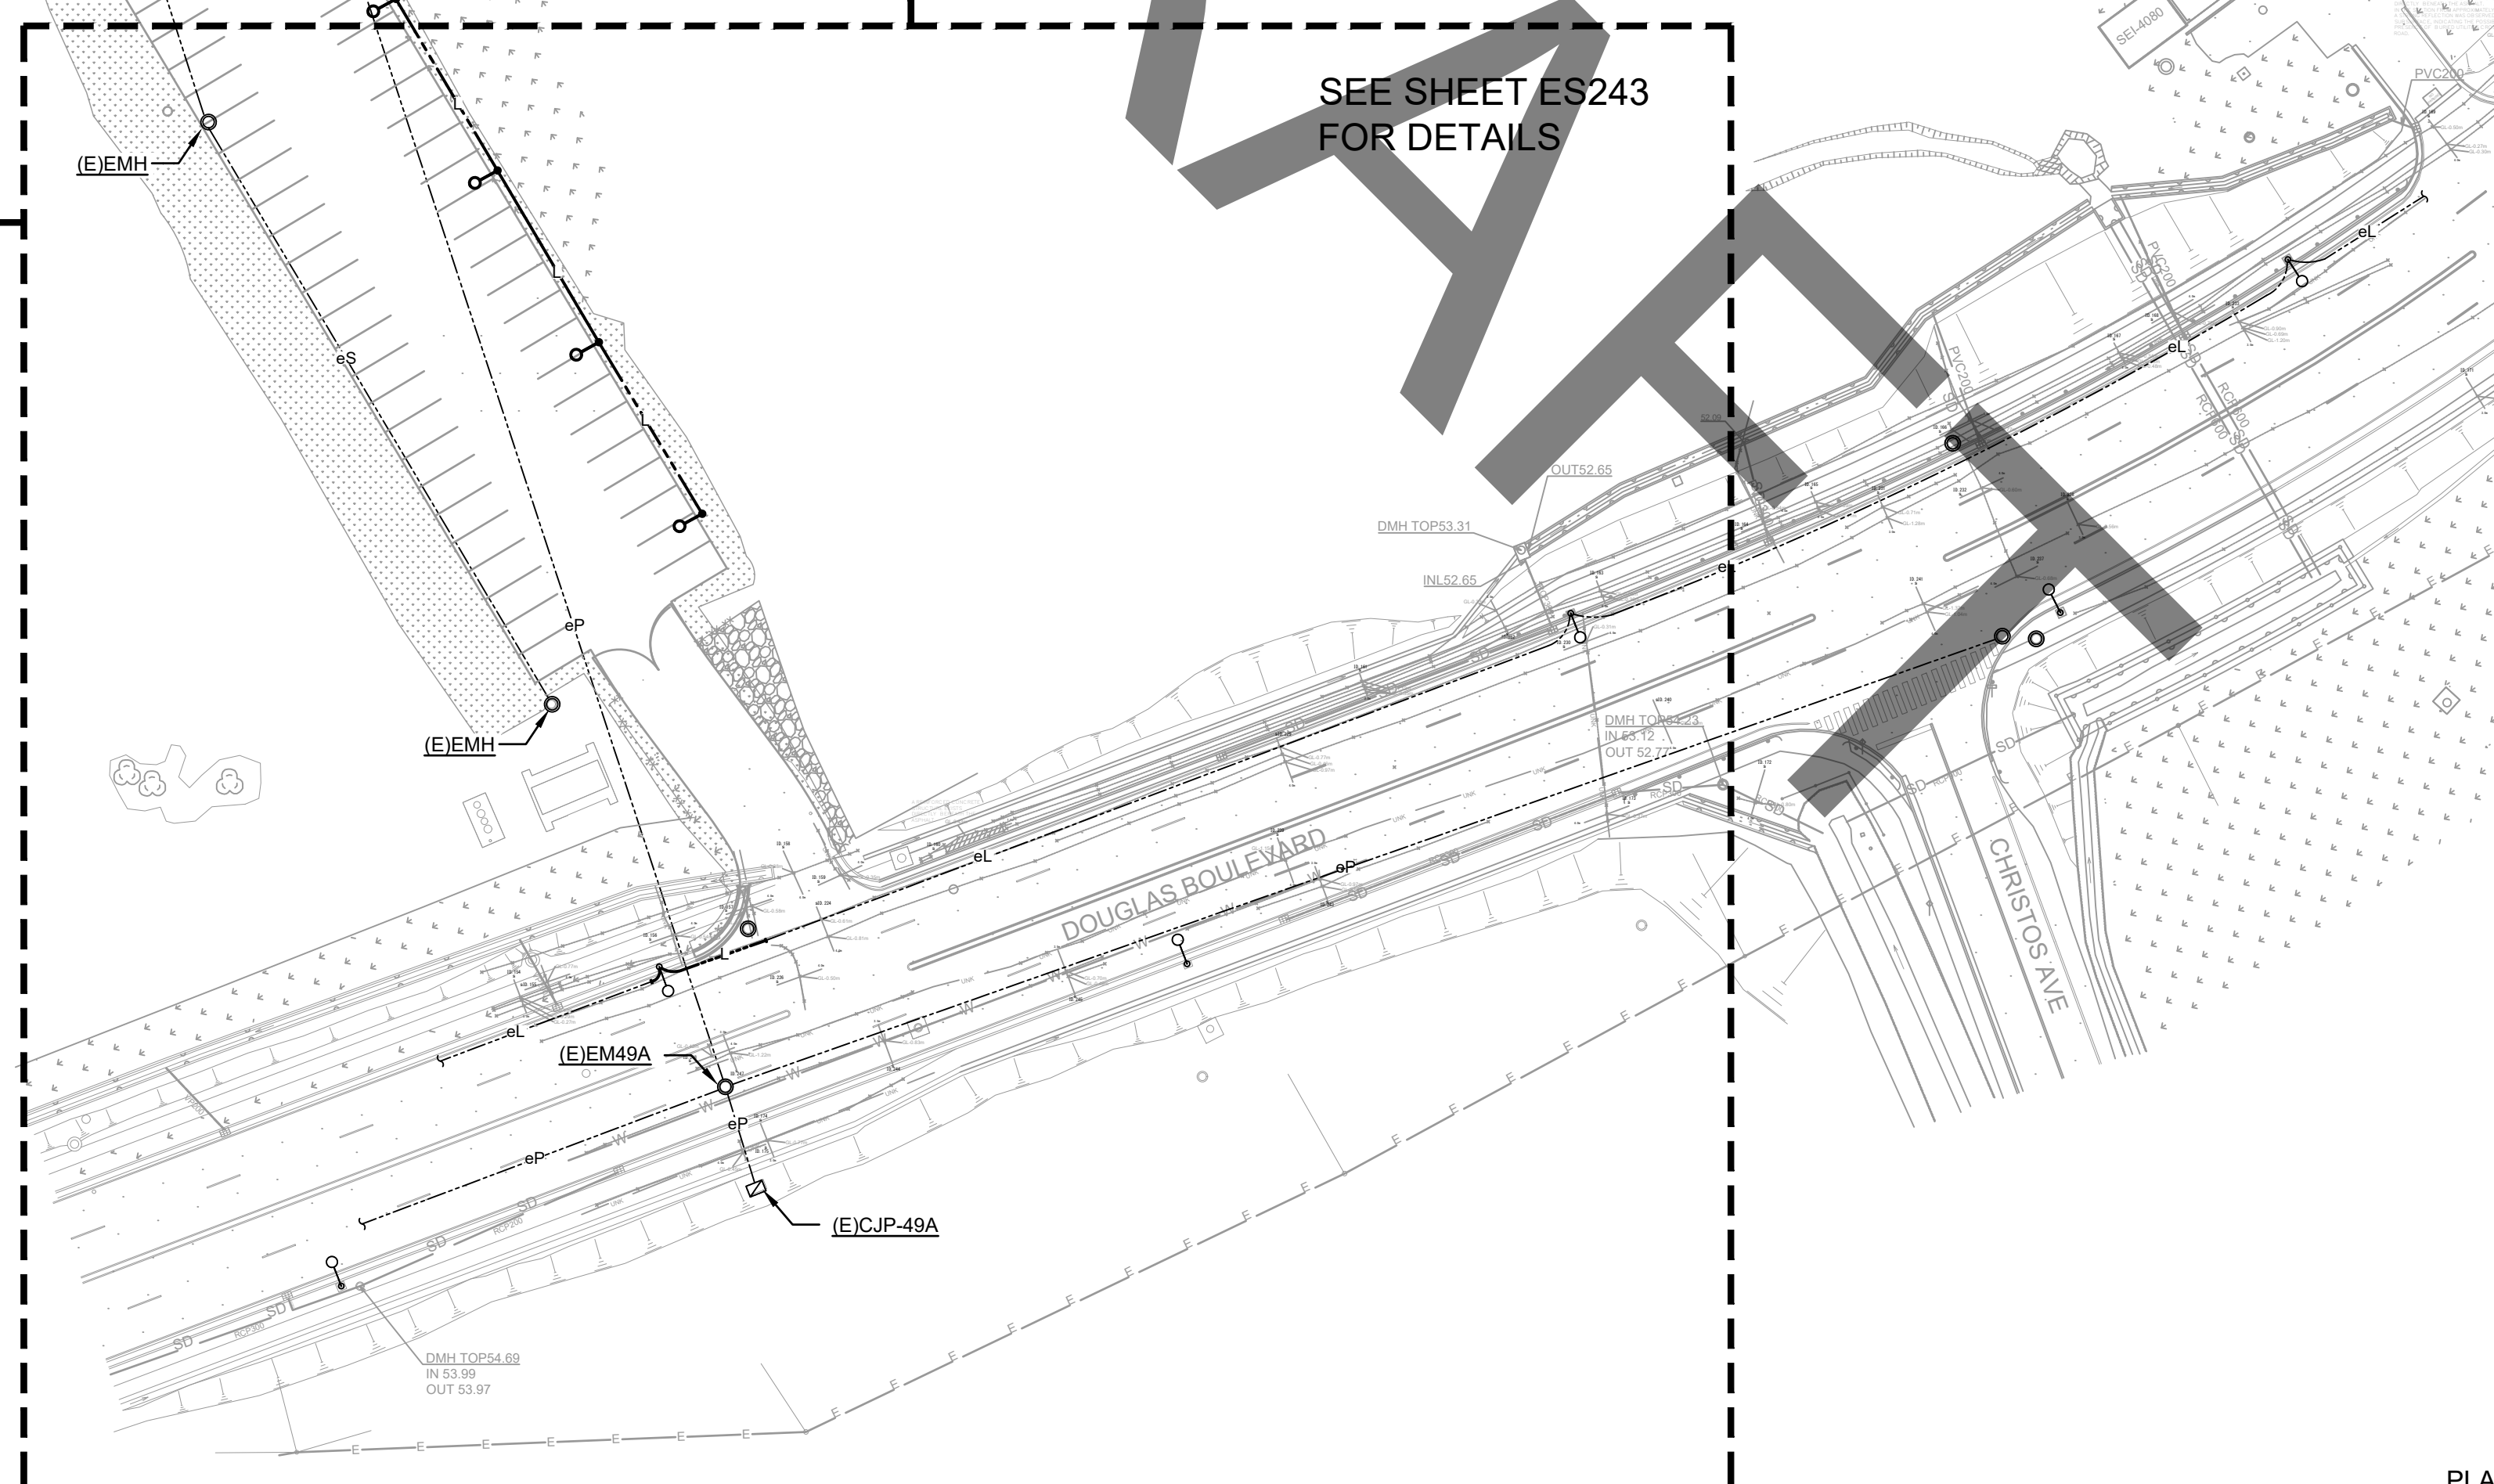

PLAN
NORTH

A circular diagram with a vertical line and a horizontal line intersecting at the center. An arrow points to the right from the center, indicating North.


0 20 40m
SCALE: 1:500

1. SEE CIVIL PLANS FOR CIVIL SITE DEMOLITION WORK AND CLOSELY COORDINATE THE ELECTRICAL DEMOLITION WORK.
2. PRIOR TO ANY ELECTRICAL EQUIPMENT AND INFRASTRUCTURE DEMOLITION WORK, ENSURE THAT THE NEW EQUIPMENT AND INFRASTRUCTURE ARE ESTABLISHED TO MINIMIZE DISRUPTION TO THE OPERATIONS OF THE EXISTING FACILITIES.
3. THE CONTRACTOR SHALL BE RESPONSIBLE TO SUBMIT A PROPOSED PHASING SCHEME FOR REVIEW AND APPROVAL PRIOR TO START OF DEMOLITION WORK.



**U.S. Army Corps
Engineers®**

[illegible]

 JAPAN DISTRICT, OKINAWA AREA OFFICE USAFD-1, UNIT 35132 APO, AP 96374-5132			SSFM INTERNATIONAL, INC. 501 SUMNER STREET, SUITE 620 HONOLULU, HAWAII 96817	
	DRAWN BY: CHECKED BY: SUBMITTED BY:	SOLICITATION NO.: CONTRACT NO.: SCALE: AS SHOWN	SIZE: ISO A1	FILE NAME:

NAZENAIR BASE, OKINAWA, JAPAN
VEHICLE MAINTENANCE SHOP
FY20 MCA PN77833

SHEET ID

ES241

INTERMEDIATE DESIGN

CLIN 0004

CLIN 0004

- CONSTRUCTION OF TEMPORARY FACILITIES AT SWING SPACE SITE MUST BE COMPLETED PRIOR TO DEMOLITION OF EXISTING ADA BUILDINGS (B4040 THRU B4047) AND SITE PREPARATION WORK FOR SSA FACILITIES.
- CONSTRUCTION OF NEW SUPPLY SUPPORT ACTIVITY (SSA) WAREHOUSE, STORAGE SHED AND ASSOCIATED ELECTRICAL INFRASTRUCTURE.
- CONSTRUCTION OF SSA PARKING LOT AND SITE LIGHTING.

P
O
N
M
L
K
J
I
H
G
F
E
D
C
B
A



A1 PARTIAL SITE ELECTRICAL PLAN 1 - COF SS (CLIN0004)
1:250

GENERAL NOTES

1. SEE CIVIL PLANS FOR CIVIL SITE DEMOLITION WORK AND CLOSELY COORDINATE THE ELECTRICAL DEMOLITION WORK.
2. PRIOR TO ANY ELECTRICAL EQUIPMENT AND INFRASTRUCTURE DEMOLITION WORK, ENSURE THAT THE NEW EQUIPMENT AND INFRASTRUCTURE ARE ESTABLISHED TO MINIMIZE DISRUPTION TO THE OPERATIONS OF THE EXISTING FACILITIES.
3. THE CONTRACTOR SHALL BE RESPONSIBLE TO SUBMIT A PROPOSED PHASING SCHEME FOR REVIEW AND APPROVAL PRIOR TO START OF DEMOLITION WORK.

KEY NOTES

- 1 EXISTING CJP-4046, CJP-4046A, SET-4046, SET-4046, DISTRIBUTION EQUIPMENT, AND ASSOCIATED FEEDERS SHALL REMAIN IN SERVICE.
- 2 EXISTING MANHOLES SHALL BE SALVAGED AND REUSED. MODIFY MANHOLE FINISH TO MATCH THE FINAL GRADING.
- 3 EXISTING CJP SHALL BE REMOVED AND REPLACED WITH NEW TO RESTORE SERVICES TO EXISTING FACILITIES AND TO FACILITATE NEW SERVICES TO THE PROPOSED BUILDINGS.
- 4 EXISTING PRIMARY FEEDER SHALL BE REMOVED AND REPLACED AND EXISTING DUCTS WILL BE UTILIZED AS A TEMPORARY SERVICE OR REMAIN AS A SPARE.

CLIN 0004

- CLIN 0004**
- CONSTRUCTION OF TEMPORARY FACILITIES AT SWING SPACE SITE MUST BE COMPLETED PRIOR TO DEMOLITION OF EXISTING ADA BUILDINGS (B4040 THRU B4047) AND SITE PREPARATION WORK FOR SSA FACILITIES.
 - CONSTRUCTION OF NEW SUPPLY SUPPORT ACTIVITY (SSA) WAREHOUSE, STORAGE SHED AND ASSOCIATED ELECTRICAL INFRASTRUCTURE.
 - CONSTRUCTION OF SSA PARKING LOT AND SITE LIGHTING.

US Army Corps of Engineers®

ISSUE DATE:		SOLICITATION NO.:		CONTRACT NO.:		SCALE:		AS SHOWN		FILE NAME:	
DESIGNED BY:	ISSUED:	DRAWN BY:	UNIT 35132	CHECKED BY:	UNIT 35132	SUBMITTED BY:	UNIT 35132	UNIT 35132	UNIT 35132	UNIT 35132	UNIT 35132

US ARMY CORPS OF ENGINEERS
JAPAN DISTRICT, OKINAWA AREA OFFICE
USAFED-J UNIT 35132
APO, AP 96374-5132

SSFM
SSFM INTERNATIONAL, INC.
501 SUMNER STREET, SUITE 620
HONOLULU, HAWAII 96817


KADENA AIR BASE, OKINAWA, JAPAN
VEHICLE MAINTENANCE SHOP
FY20 MCA PN77833

PARTIAL SITE ELECTRICAL PLAN 1 - COF SS (CLIN 0004)


SHEET ID

ES242

INTERMEDIATE DESIGN

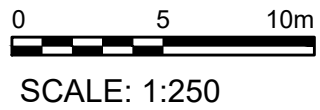

1. SEE CIVIL PLANS FOR CIVIL SITE DEMOLITION WORK AND CLOSELY COORDINATE THE ELECTRICAL DEMOLITION WORK.
2. PRIOR TO ANY ELECTRICAL EQUIPMENT AND INFRASTRUCTURE DEMOLITION WORK, ENSURE THAT THE NEW EQUIPMENT AND INFRASTRUCTURE ARE ESTABLISHED TO MINIMIZE DISRUPTION TO THE OPERATIONS OF THE EXISTING FACILITIES.
3. THE CONTRACTOR SHALL BE RESPONSIBLE TO SUBMIT A PROPOSED PHASING SCHEME FOR REVIEW AND APPROVAL PRIOR TO START OF DEMOLITION WORK.

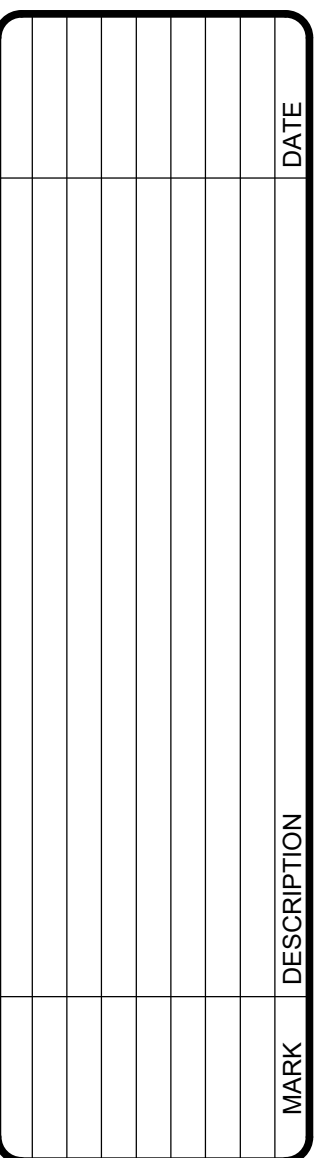

1	RELOCATED STREET LIGHT. PROVIDE NEW FOUNDATION TO MATCH EXISTING.
2	INTERCEPT EXISTING DUCT AND EXTEND IT TO RELOCATED POLE FOUNDATION. PROVIDE NEW CIRCUIT TO RESTORE THE OPERATION.

US ARMY CORPS OF ENGINEERS JAPAN DISTRICT, OKINAWA AREA OFFICE USAED-J UNIT 35132 APO, AF 96374-5132	DESIGNED BY:	ISSUE DATE:
	DRAWN BY:	SOLICITATION NO.:
	CHECKED BY:	CONTRACT NO.:
	SUBMITTED BY:	SCALE: AS SHOWN
 SSFM INTERNATIONAL, INC. 507 SUMNER STREET, SUITE 620 HONOLULU, HAWAII 96817	FILE NAME:	
	SIZE: A1	

CLIN 0004

- CONSTRUCTIO OF TEMPORARY FACILITIES AT SWING SPACE SITE MUST BE COMPLETED PRIOR TO DEMOLITION OF EXISTING ADA BUILDINGS (B4040 THRU B4047) AND SITE PREPARATION WORK FOR SSA FACILITIES.
- CONSTRUCTION OF NEW SUPPLY SUPPORT ACTIVITY (SSA) WAREHOUSE, STORAGE SHED AND ASSOCIATED ELECTRICAL INFRASTRUCTURE.
- CONSTRUCTION OF SSA PARKING LOT AND SITE LIGHTING.

KADENA AIR BASE, OKINAWA, JAPAN
VEHICLE MAINTENANCE SHOP
FY20 MCA PN77833

SHEET ID

ES243

INTERMEDIATE DESIGN




1. CONCRETE ENCASED CONDUITS SHALL BE PVC SCHEDULE 40.
2. PROVIDE ALL EMPTY CONDUITS WITH PULLWIRE. PROVIDE ALL EMPTY COMMUNICATIONS CONDUIT WITH MULETAPE .
3. AT LANDSCAPED AREAS RESTORE SURFACES TO MATCH EXIST ADJACENT SURFACES.
4. 5 MIL THICK ORANGE (TELECOMMUNICATIONS) COLORED PLASTIC WARNING TAPE 75MM WIDE, ENTIRE LENGTH OF DUCT. TAPE TO HAVE CONTINUOUS METALLIC BACKING AND CORROSION RESISTANT FOIL CORE. WARNING AND IDENTIFICATION TO BE IMPRINTED ON TAPE AND SHALL READ "CAUTION BURIED TELECOMMUNICATIONS CABLE BELOW". MESSAGE SHALL RE REPEATED APPROXIMATELY EVERY 3050MM.

BACKFILL NOTES:

TYPE "A" BACKFILL - EARTH & GRAVEL.
ROCK SIZE TO BE 25mm MAX & THE
MIXTURE TO CONTAIN NOT MORE
THAN 50% BY VOLUME OF ROCK
PARTICLES. 95% COMPACTION.

CONCRETE - 75mm ENCASEMENT,
2500 PSI COMPRESSIVE STRENGTH
@ 28 DAYS.

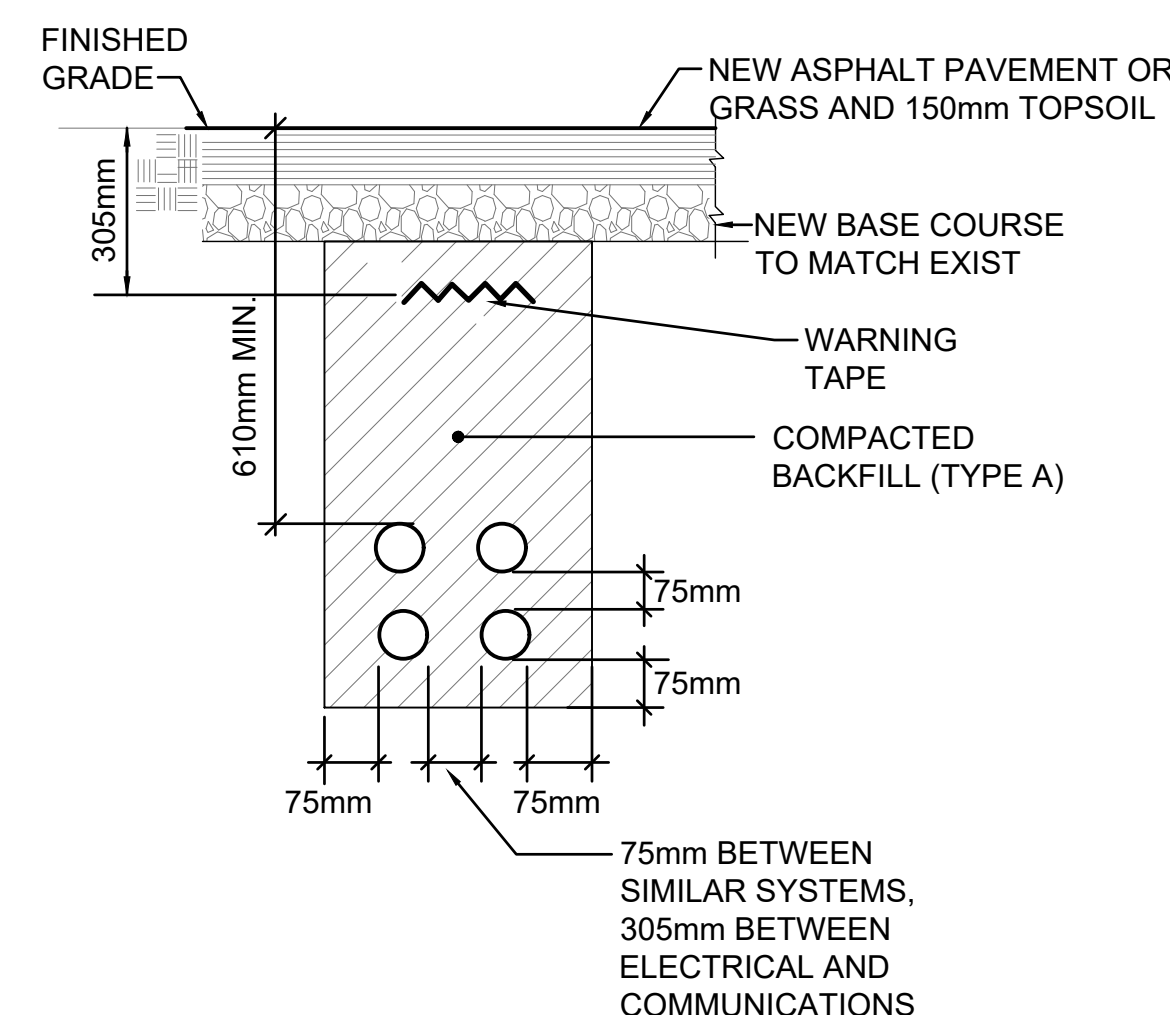


DUCT NOTES:

1. ALL CONDUITS SHALL BE PVC SCHEDULE 80 UNLESS NOTED OTHERWISE.
2. ALL CONDUITS SHALL CONTAIN A POLYOLEFIN PULL LINE (JET LINE CAT. #232 OR EQUIVALENT).
3. AFTER INSTALLATION OF CONDUITS, A SMOOTH BULLET-SHAPED WOODEN TEST MANDREL IS TO BE PASSED THROUGH THE ENTIRE LENGTH OF EACH CONDUIT TO TEST FOR FREEDOM OF BURRS AND OBSTRUCTIONS.
4. BACKFILL LEGEND:

TYPE "A" BACKFILL
BEACH SAND, EARTH, OR EXPOSED
IF EARTH EXPOSED, THE MATERIAL
SHALL BE 25.4mm AND THE
CONTAIN NOT MORE THAN
OF ROCK PARTICLES. 90%
5. SAWCUT EXIST CONCRETE AND A.C. PAVEMENT PRIOR TO TRENCHING. PATCH AND REPAIR TO MATCH EXISTING.
6. WARNING TAPE: BRIGHTLY COLORED PLASTIC TAPE, 8 MIL THICKNESS, NOT LESS THAN 101MM IN WIDTH WITH METALLIC BACKING. APPROXIMATELY 304MM BELOW FINISHED GRADE.

CONCRETE ENCASED DUCT DETAILS

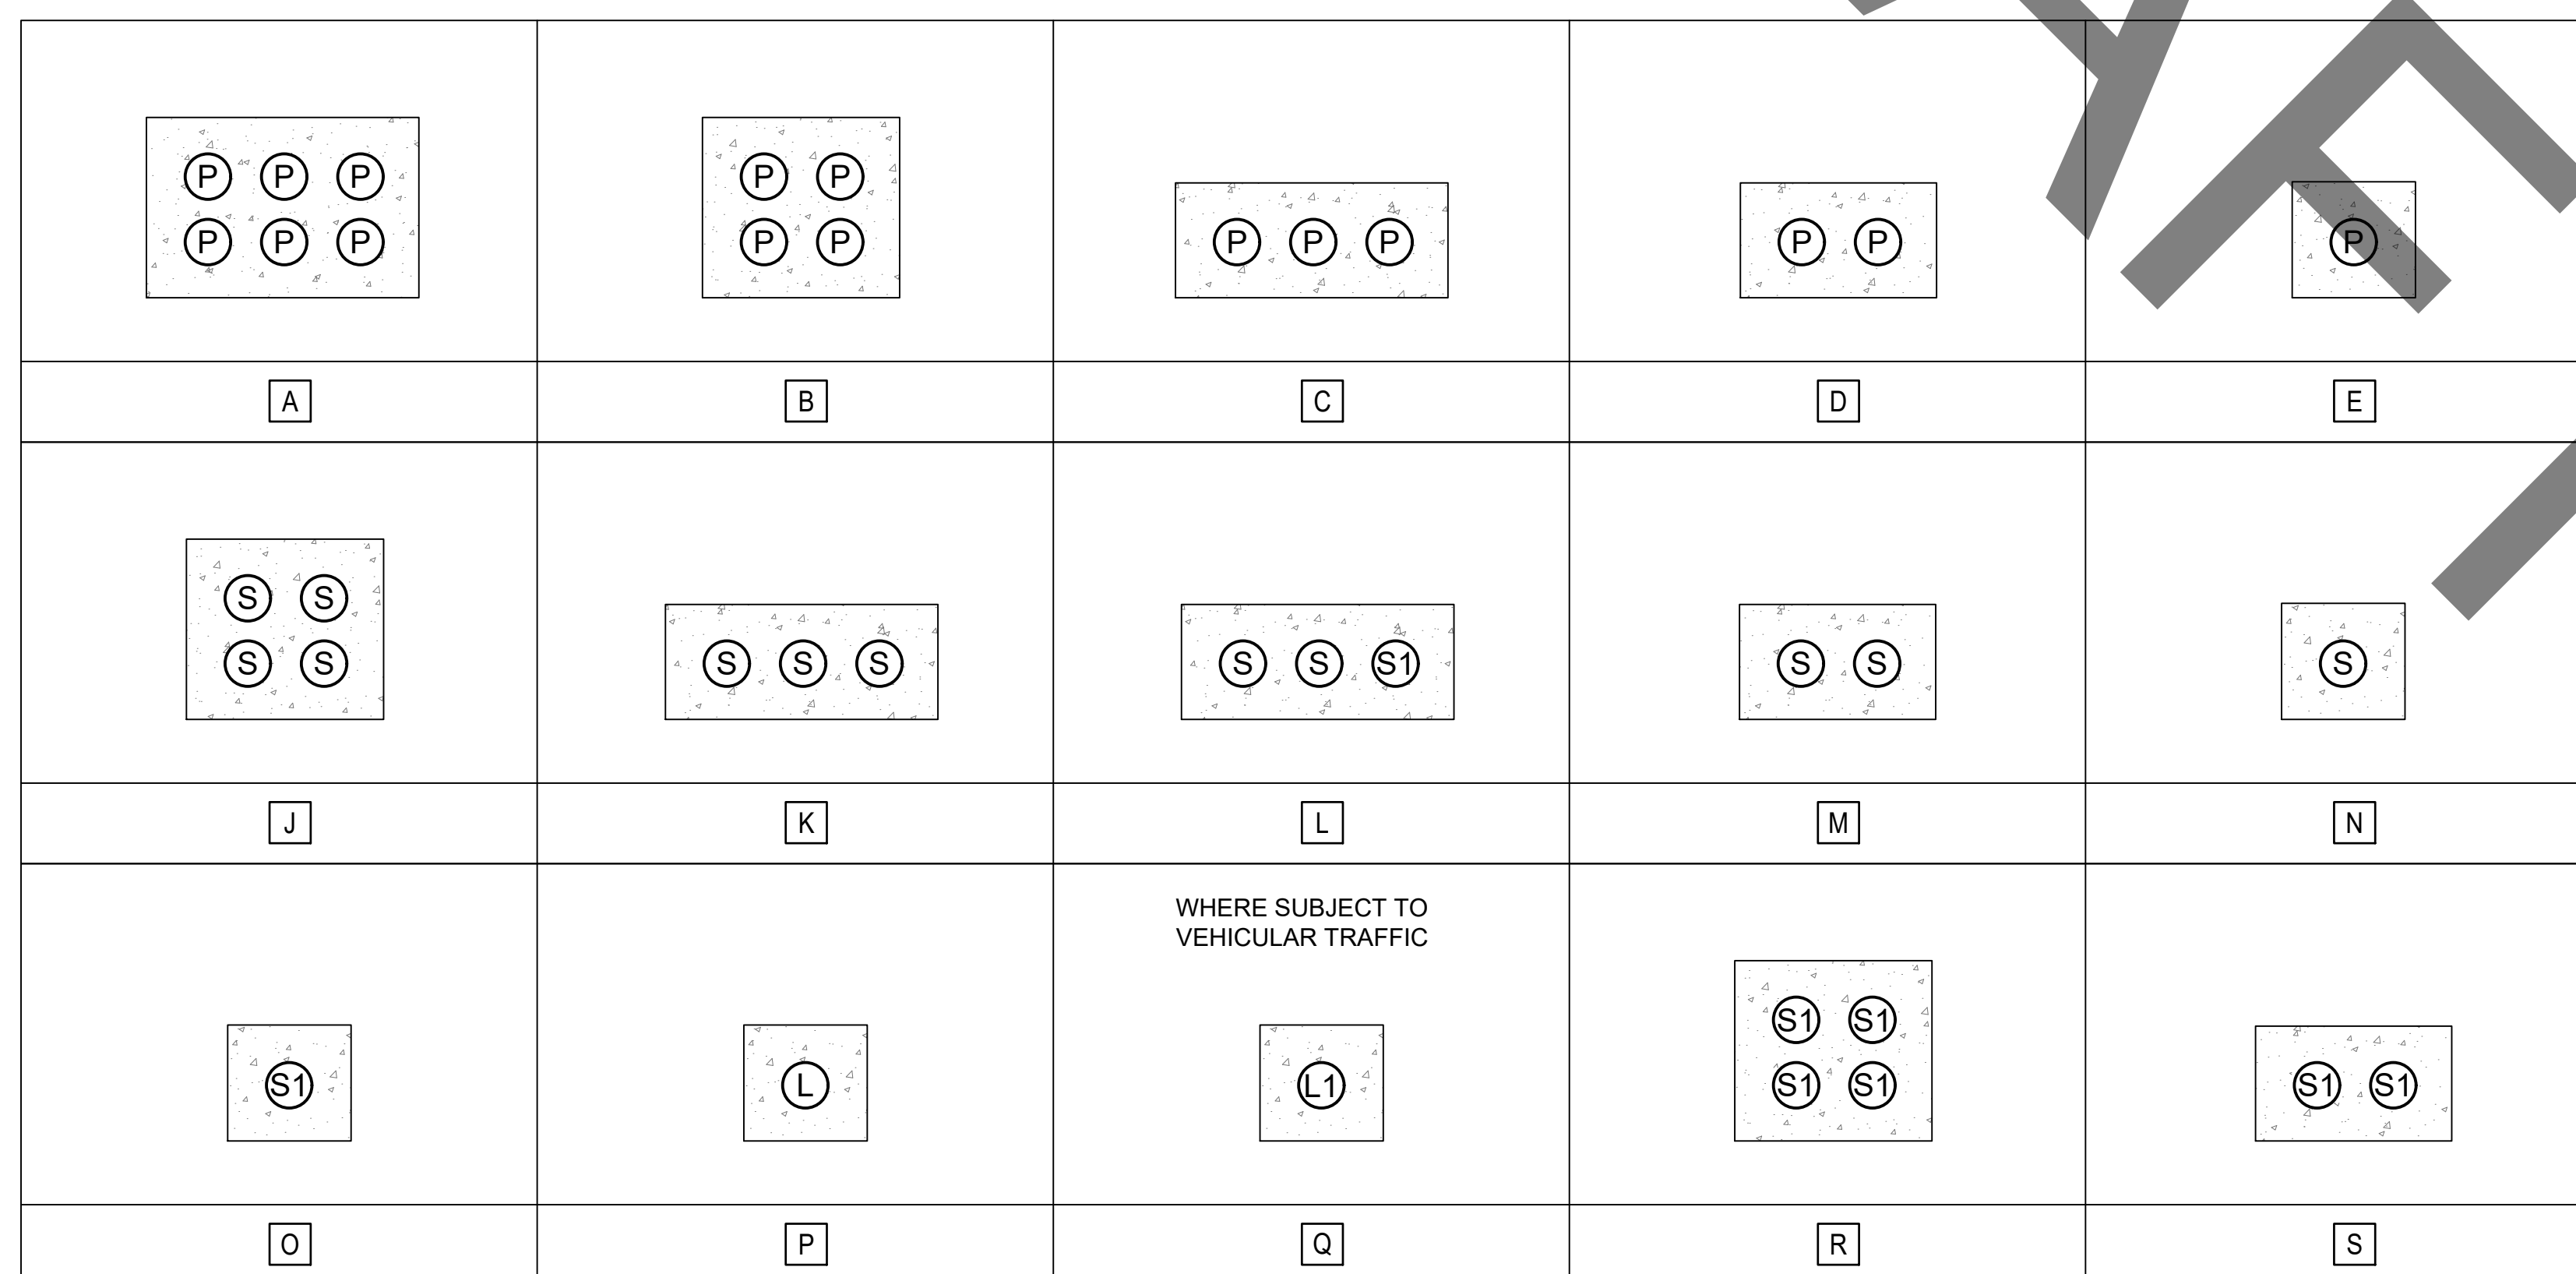


DIRECT BURIED DUCT DETAILS



DUCT SCHEDULE	
TYPE	DESCRIPTION
P	125C: PRIMARY DUCT
S	104C: SECONDARY DUCT
SP	104C: SECONDARY DUCT SPARE
S1	53C: SECONDARY DUCT
L	53C: LIGHTING DUCT
L1	27C: LIGHTING DUCT

NOTE:

COORDINATE PLACEMENT OF NEW DUCT WHERE IT IS INSTALLED ALONG EXISTING DUCT, AND ENSURE IT TO MEET THE REQUIRED BURIAL DEPTH AND LOCATION OF PENETRATION INTO EXIST MANHOLE.

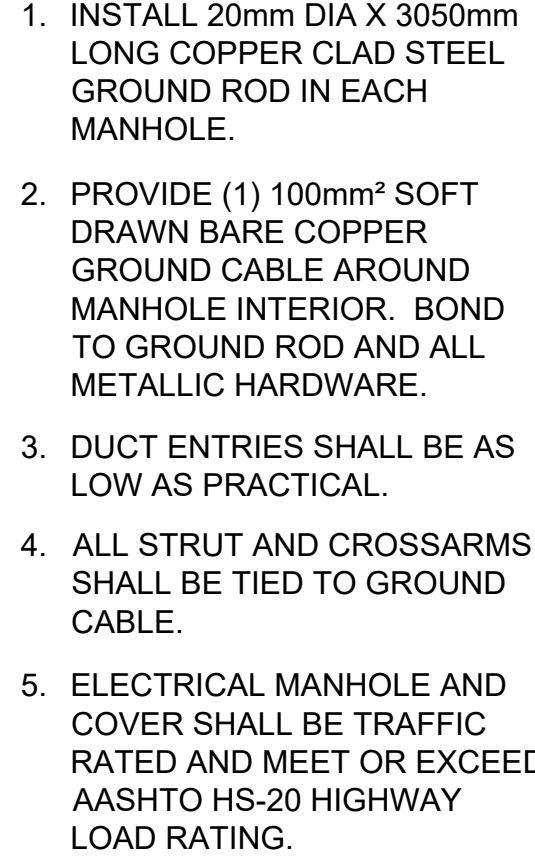

—
O —
N —
M —
L —
K —
J —
I —
H —
G —
F —
E —
D —
C —
B —
A

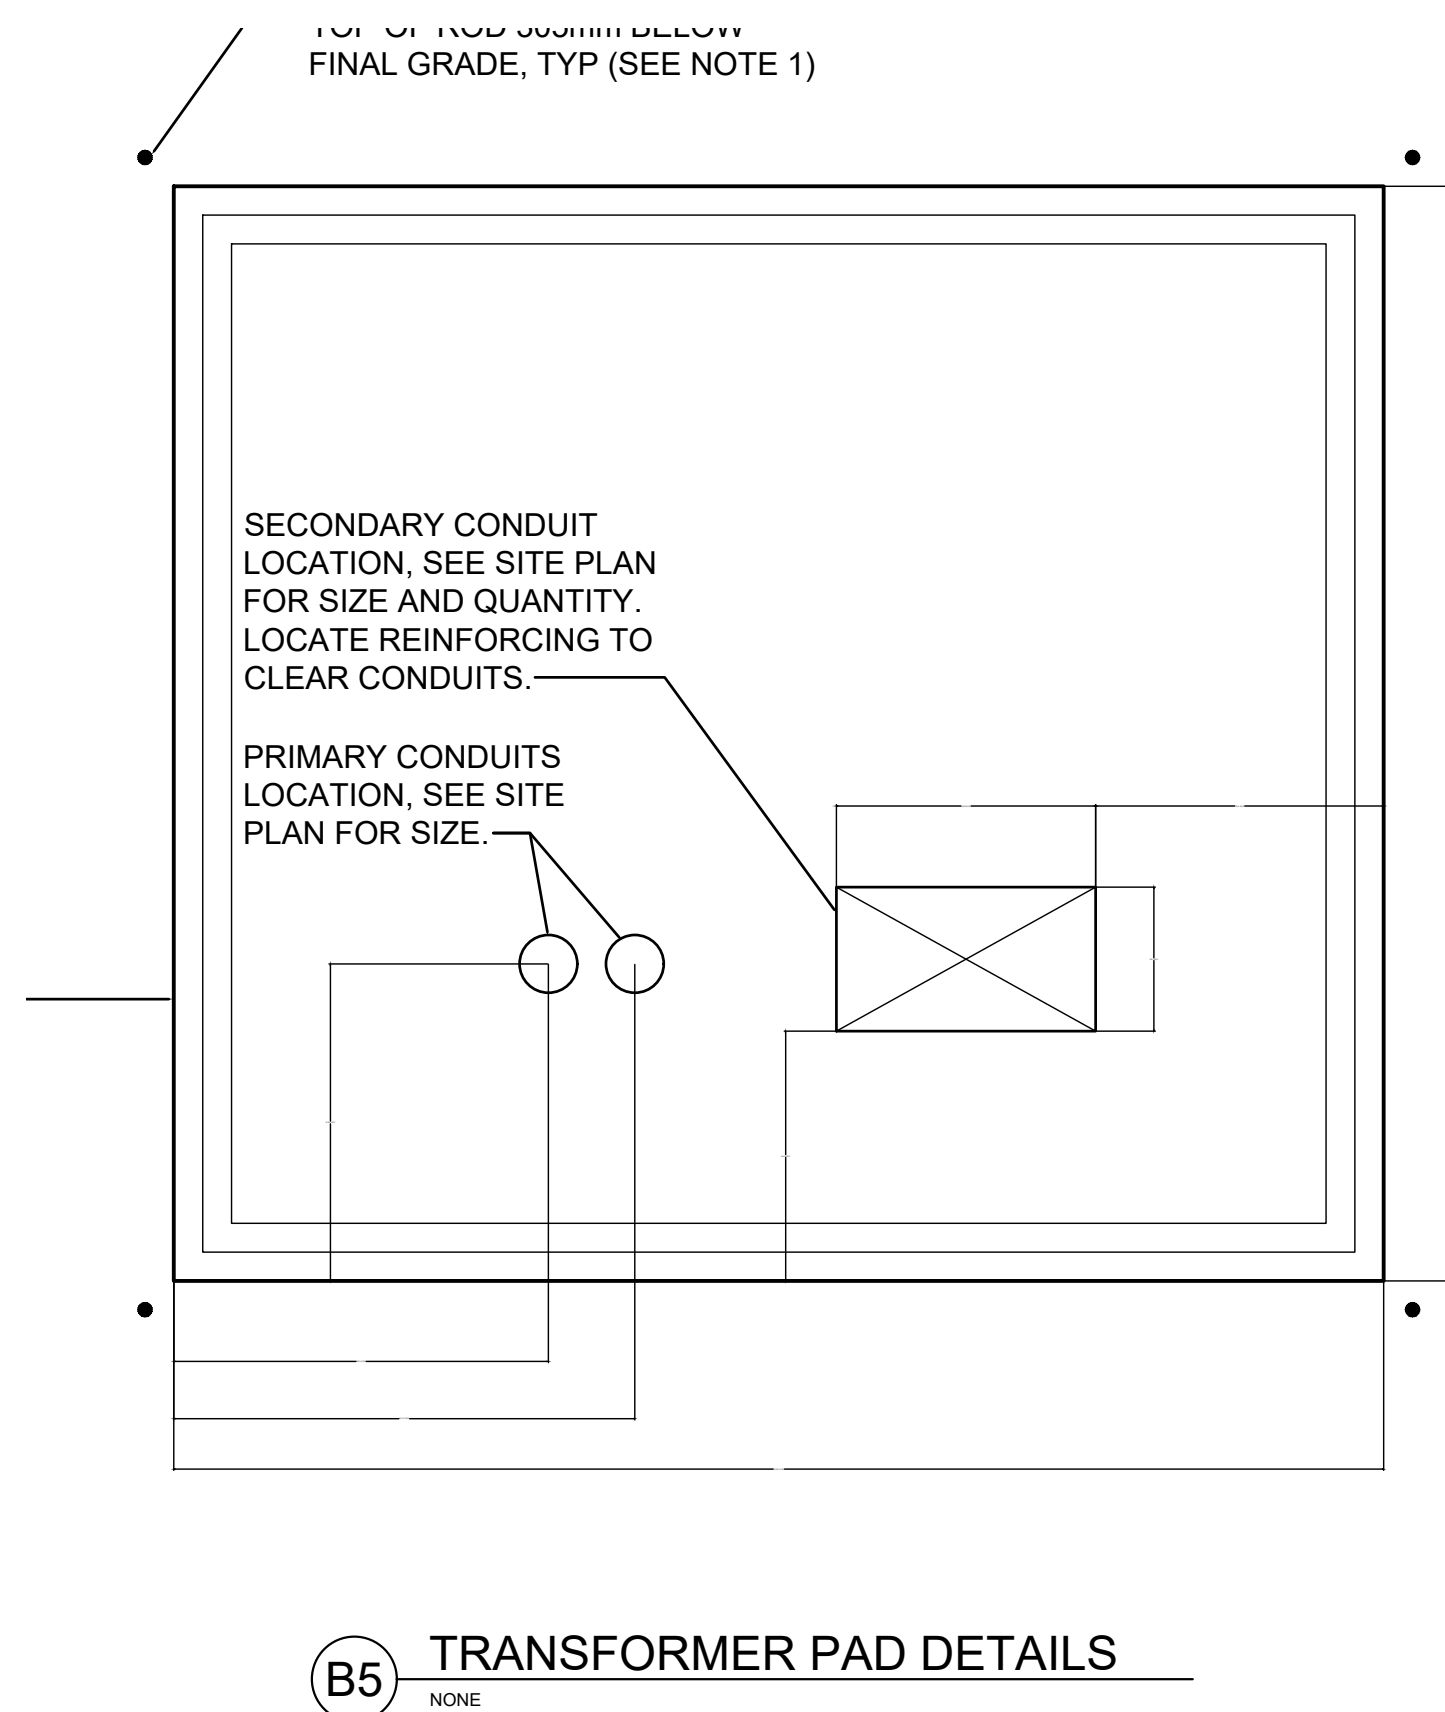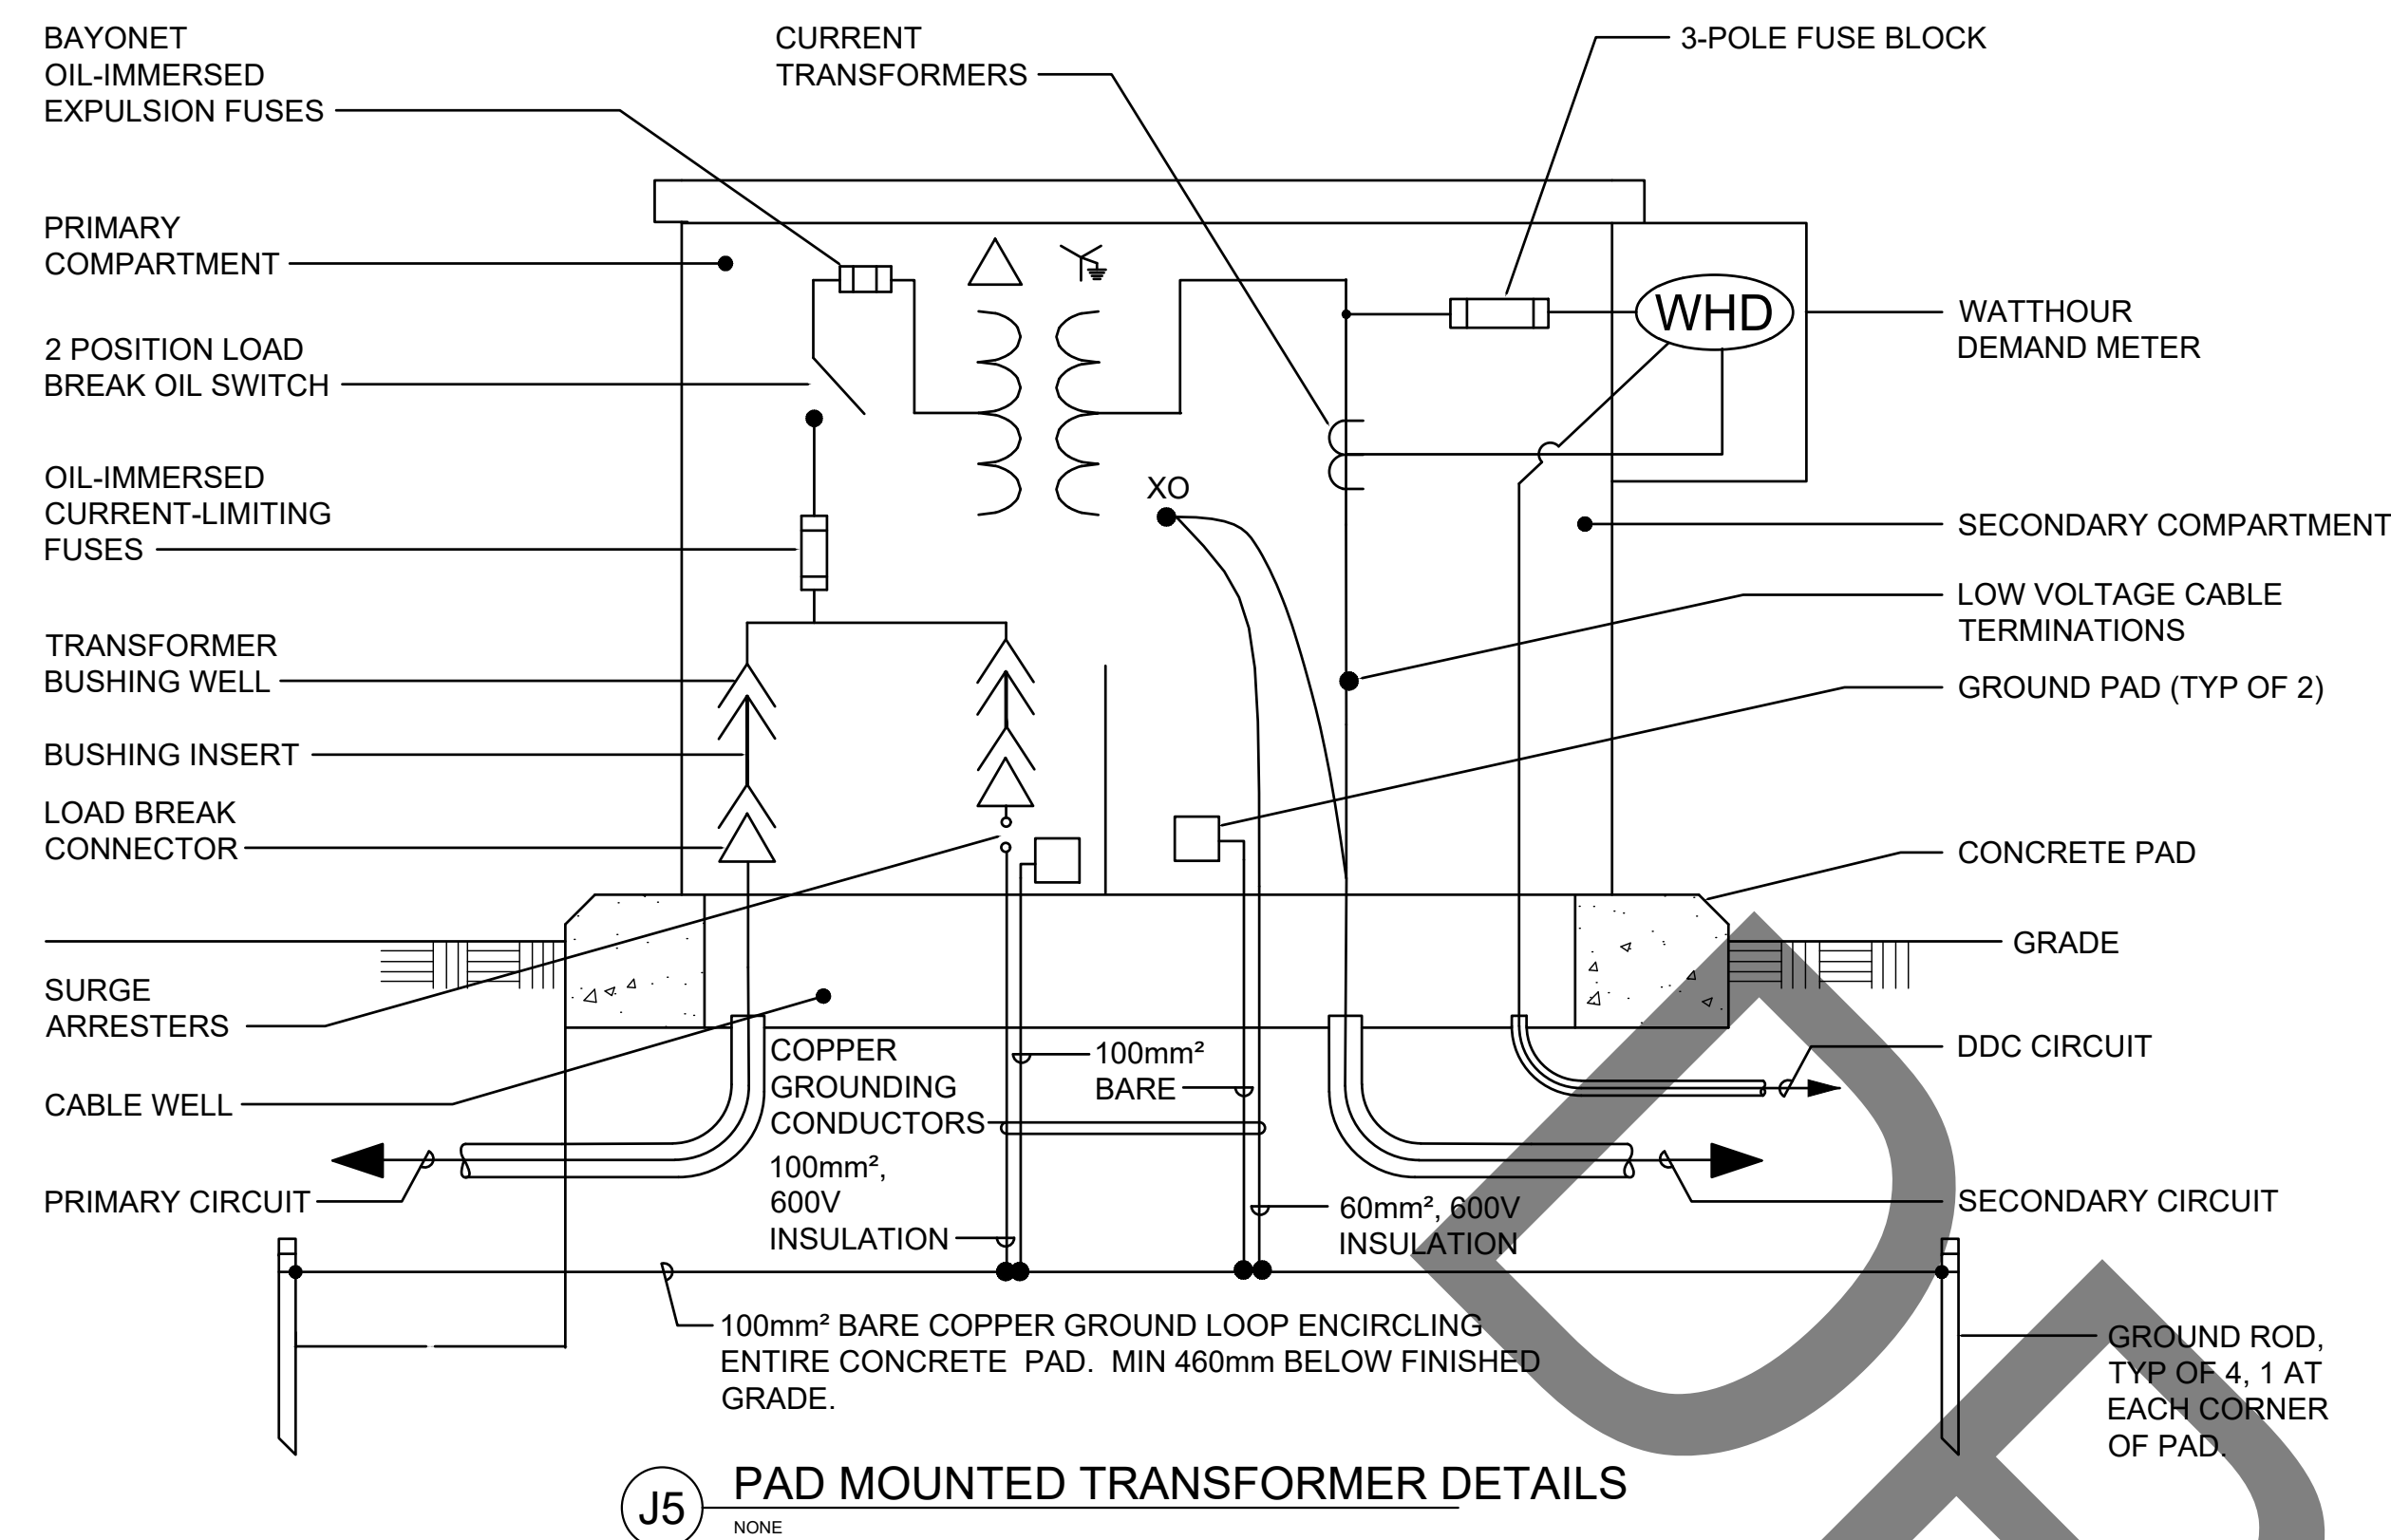

- NOTES:**
1. 20mm DIA. x 3050mm GROUND ROD. IF GROUND RESISTANCE IS MORE THAN 25 OHMS, INSTALL ADDITIONAL 20mm DIA. x 3050mm GROUND ROD AND CONNECT 100mm² BARE COPPER GROUND WIRE BETWEEN GROUND RODS. A MINIMUM OF 1830mm SHALL BE MAINTAINED BETWEEN THE DRIVEN GROUND RODS.
 2. CONCRETE: 30 Mpa COMPRESSIVE STRENGTH IN 28 DAYS. MOISTURE CURE CONCRETE PAD A MINIMUM OF 7 DAYS. DO NOT INSTALL TRANSFORMER UNTIL CONCRETE COMPRESSIVE STRENGTH REACHES 10.3 Mpa MINIMUM OR AFTER 14 DAYS.
 3. REINFORCING: SEE STRUCTURAL DRAWINGS FOR REINFORCING DETAILS.
 4. LOCATE, SECURE, AND CAP ALL CONDUITS BEFORE POURING PAD. TOP OF CONCRETE TO BE SMOOTH AND TRUE, WOOD-FLOAT FINISH, FREE OF DEFECTS, AS PER SPECIFICATIONS. ROUND ALL EXPOSED EDGES TO 20mm CHAMFER.
 5. MAINTAIN A RELATIVELY LEVEL, MINIMUM CLEARANCE OF 762mm FROM THE SIDE OF THE PAD, 610mm FROM THE BACK OF PAD, AND 2440mm IN FRONT OF PAD.
 6. CONCRETE PAD DIMENSIONS AND OPENINGS SHALL BE ADJUSTED AS REQUIRED TO ACTUAL TRANSFORMER REQUIREMENTS.
 7. CONCRETE PAD SHALL HAVE WOOD FLOAT FINISH.

- TRANSFORMER NOTES:
1. ENCLOSURE SHALL BE STAINLESS STEEL, NEMA 4X.
 2. ENCLOSURE SHALL BE FACTORY PAINTED, NORWOOD BROWN FEDERAL #10045.
 3. PROVIDE LABEL ON TRANSFORMER PER BASE REQUIREMENTS.



**U.S. Army Corps
Engineers®**

[illegible]

JAPAN DISTRICT, OKINAWA AREA OFFICE		SOLICITATION NO.:	
USAEJ-J Unit 35132		DRAWN BY:	
APO, AP 96337-41532		CHECKED BY:	
 SSPM INTERNATIONAL, INC. 500 KALANIANA'OLUHIMA DRIVE, SUITE 220 HONOLULU, HAWAII 96817		CONTRACT NO.:	
		SUBMITTED BY:	
		AS SHOWN	
ISO A1	SIZE:	FILE NAME:	

PAD MOUNTED TRANSFORMER DETAILS

SHEET ID

ES503

INTERMEDIATE DESIGN

[illegible]





JAPAN DISTRICT, OKINAWA AREA OFFICE USAED-J UNIT 35132 APO, AP 96374-5132		SSFM INTERNATIONAL, INC 501 SUMMER STREET, SUITE 620
	DRAWN BY:	SOLICITATION NO.:
	CHECKED BY:	CONTRACT NO.:
	SUBMITTED BY:	SCALE: AS SHOWN
SIZE: .	FILE NAME:	

CABLE JUNCTION PEDESTAL (CJP) DETAILS


SHEET ID

ES504

INTERMEDIATE DESIGN

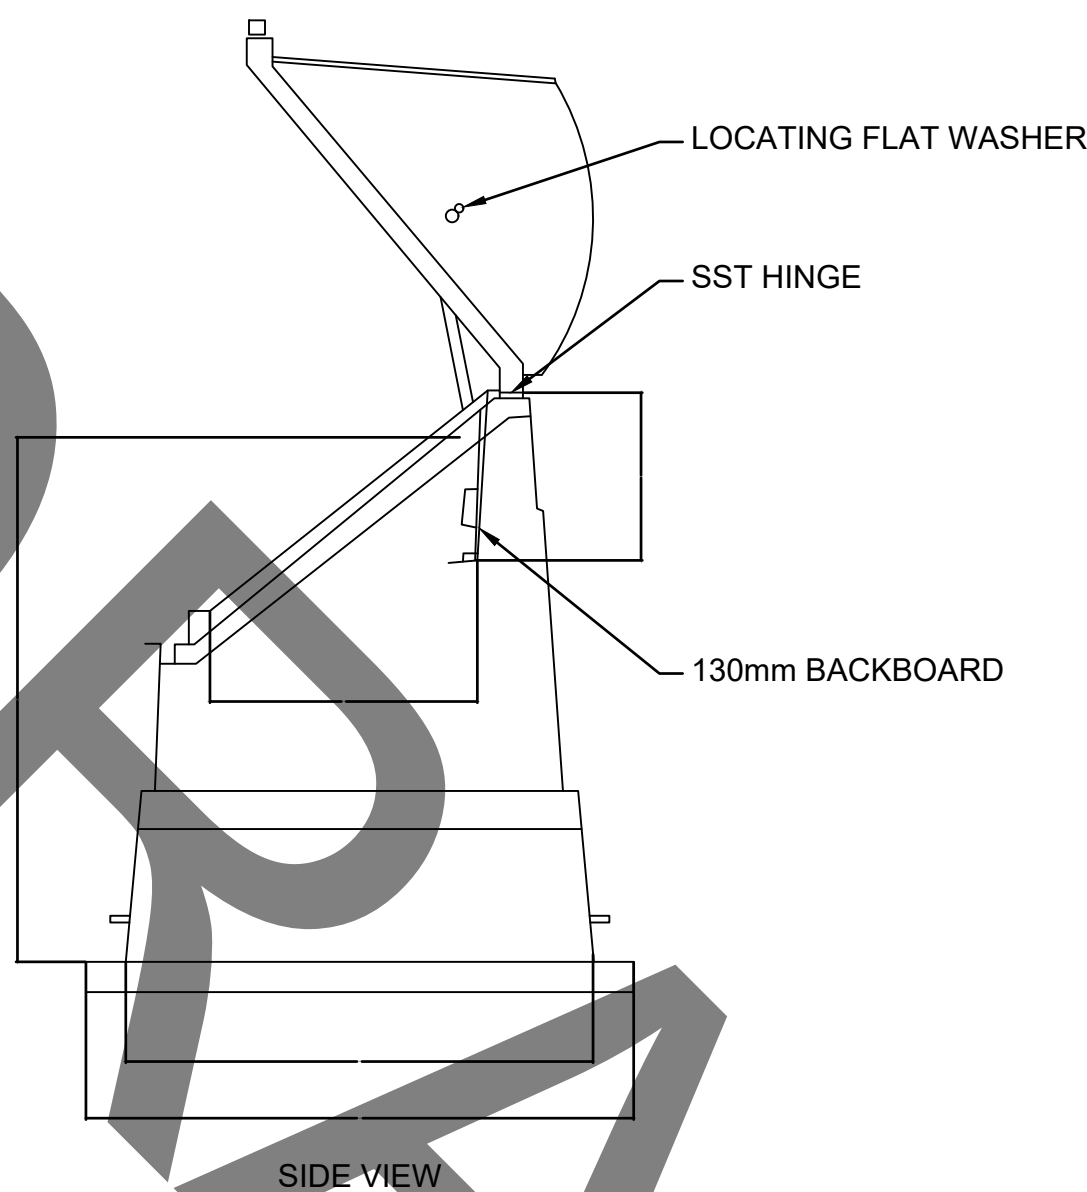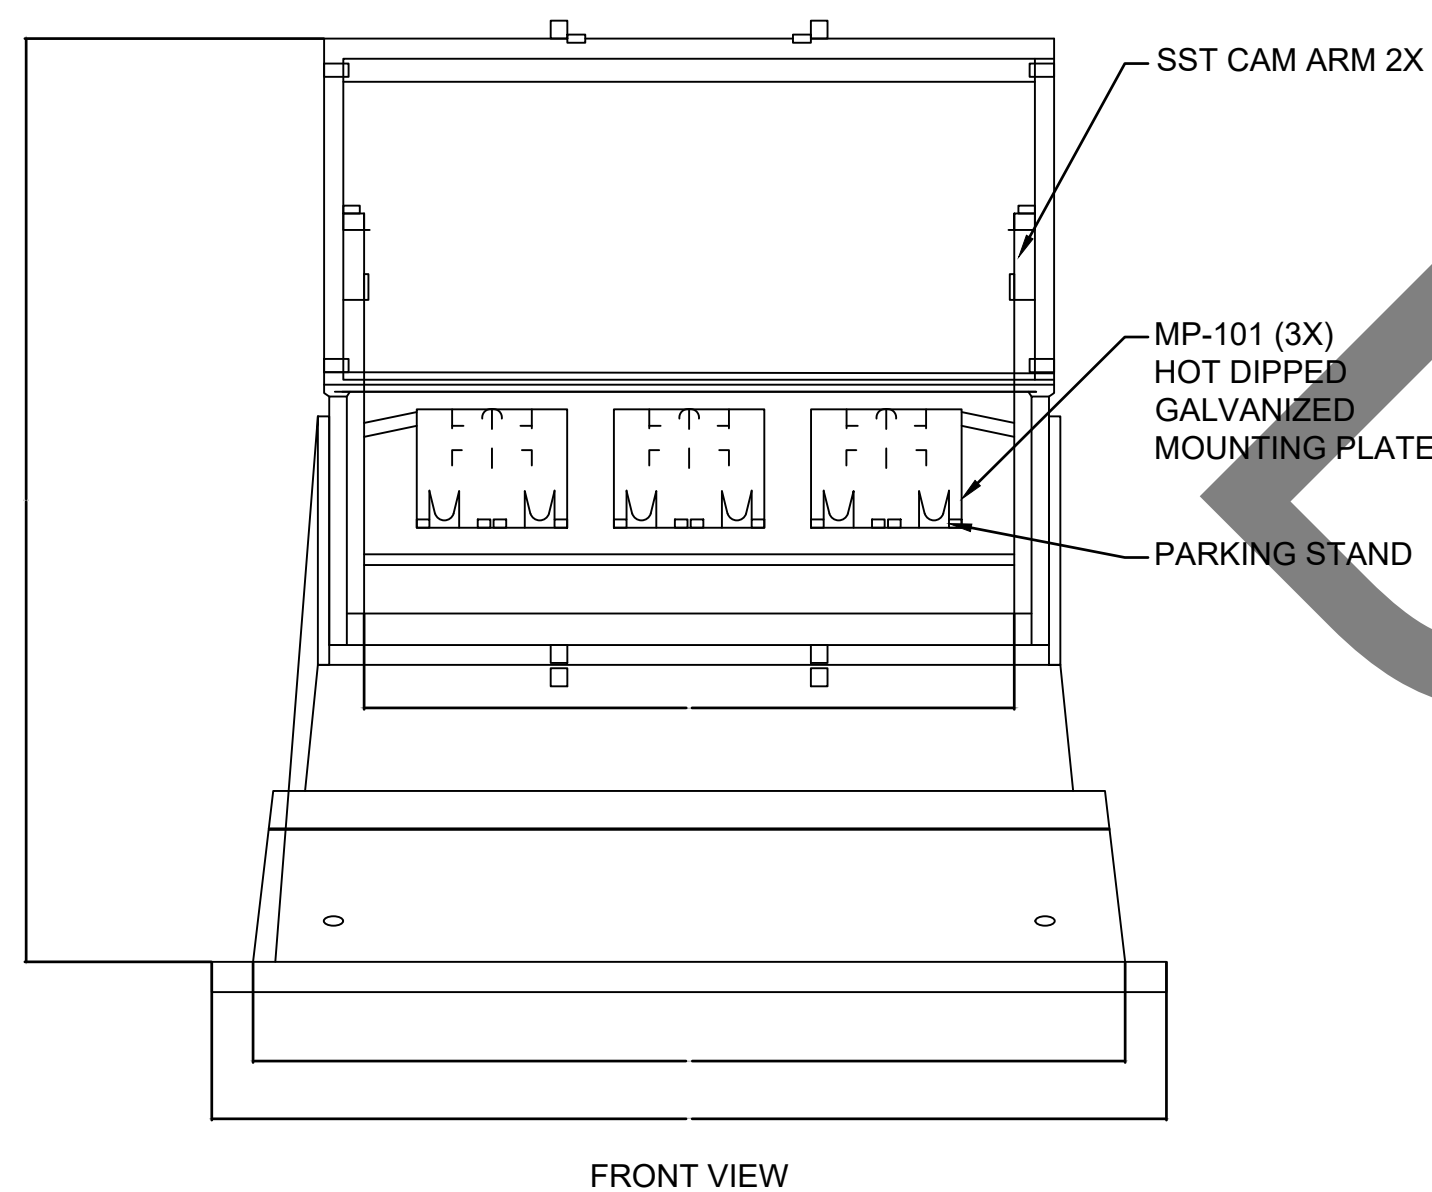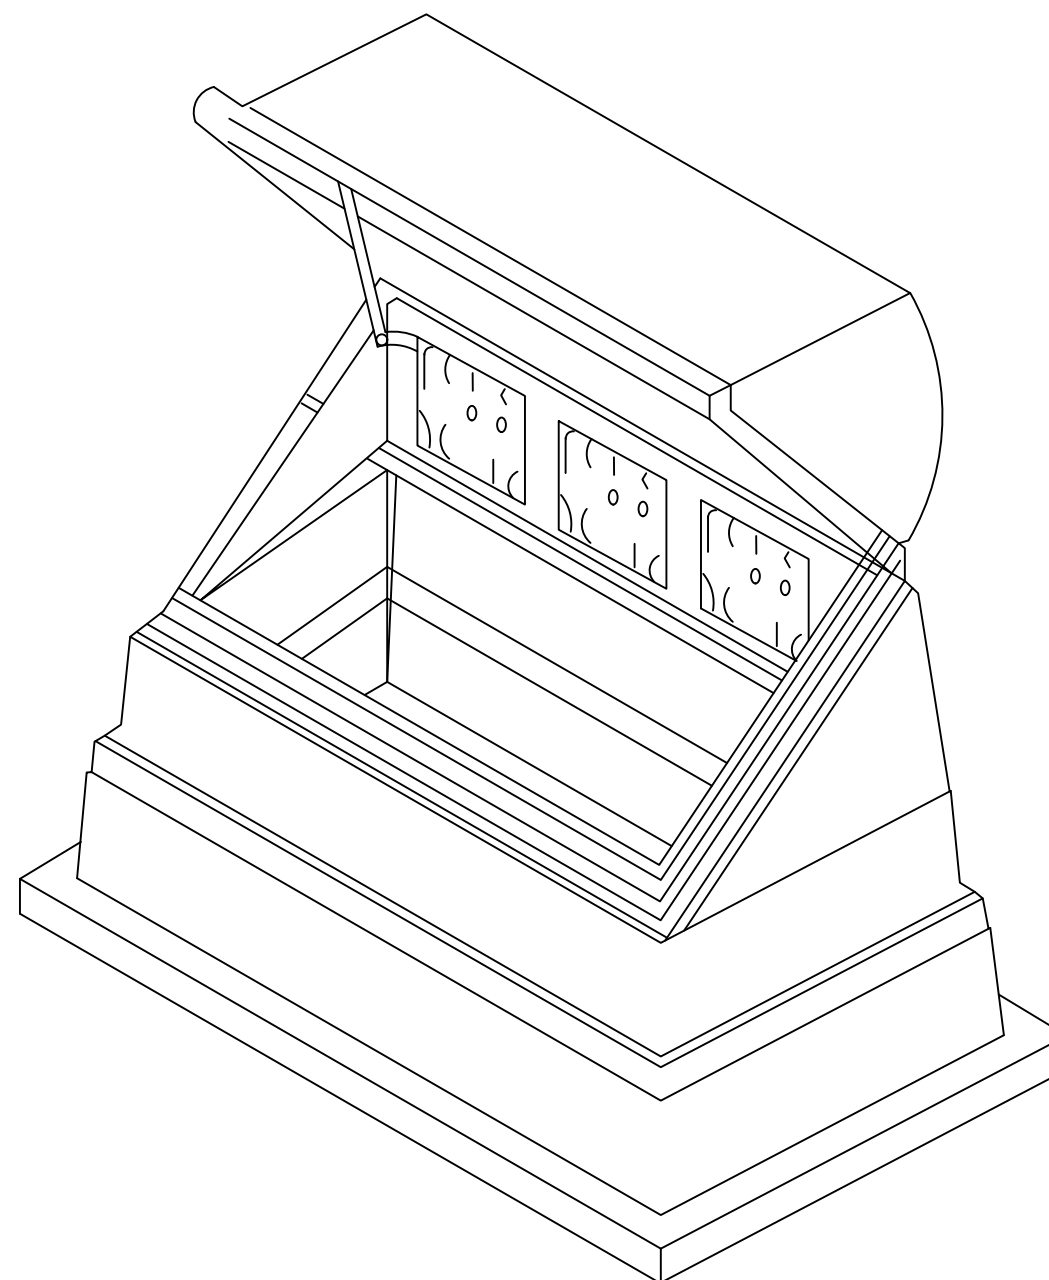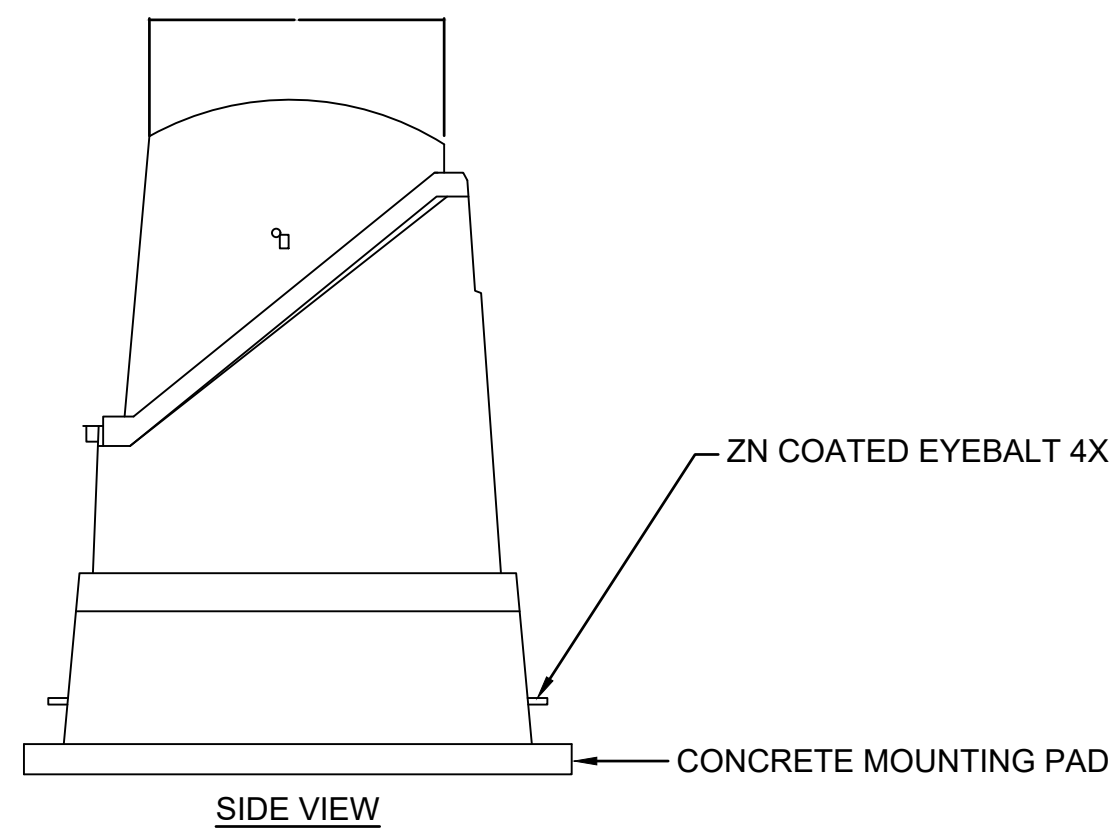


ENCLOSURE

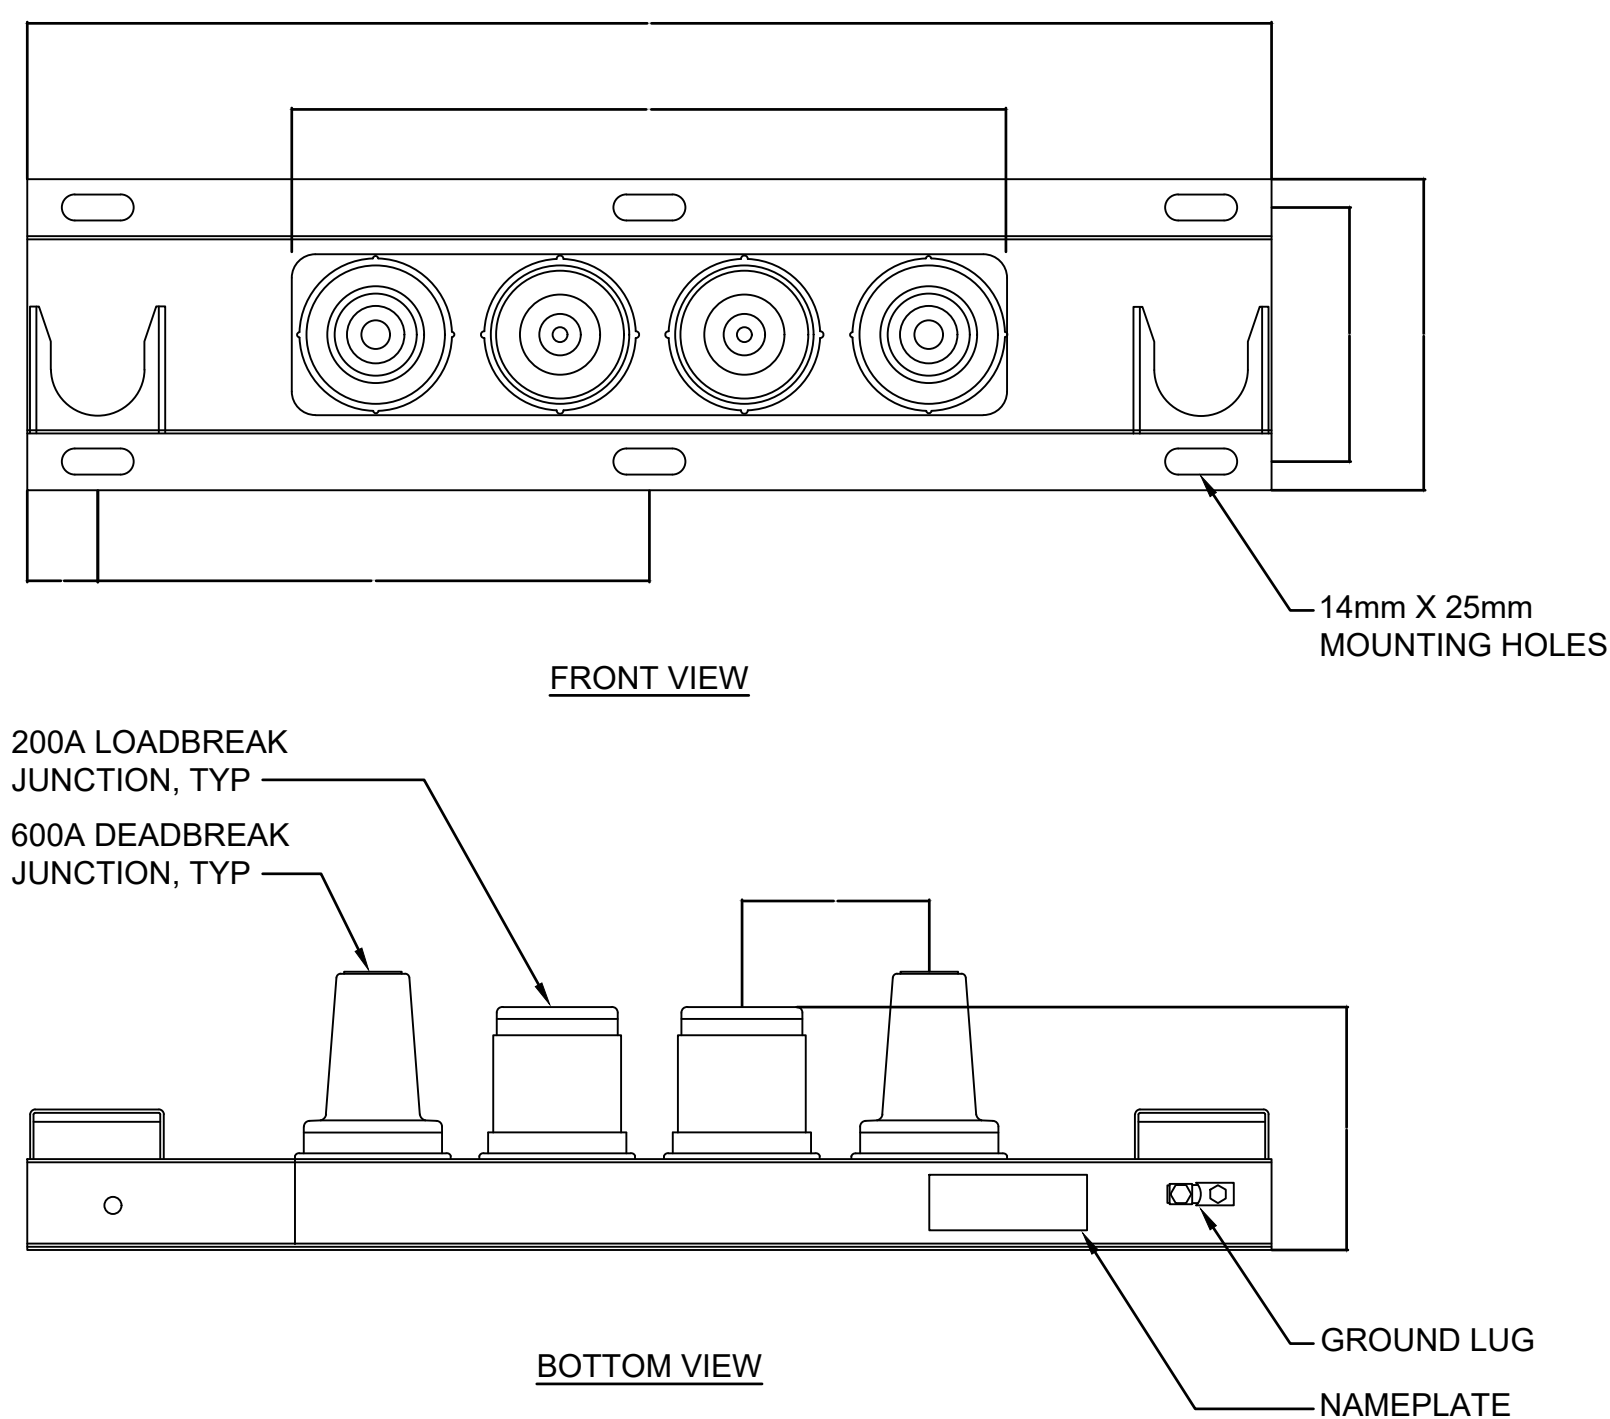

MULTI-POINT JUNCTION

- NOTES:**
1. ENCLOSURE SHALL BE MADE OF HEAVY DUTY, REINFORCED FIBERGLASS. RATED FOR 600A, 15KV.
 2. ENCLOSURE SHALL ACCOMMODATE THREE (3) 4-POINT 15KV MULTI-POINT JUNCTIONS WITH U-STRAPS.
 3. MULTI-POINT JUNCTIONS SHALL HAVE MINIMUM OF TWO (2) 600A, 15KV DEADBREAKS AND TWO (2) 200A, 15KV LOADBREAKS.
 4. MULTI-POINT JUNCTIONS SHALL INCORPORATE LIGHTWEIGHT, DAMAGE RESISTANT, EPDM MOLDED RUBBER CONSTRUCTION AND CORROSION RESISTANT 304 STAINLESS STEEL MOUNTING BRACKETS. JUNCTIONS SHALL BE MAINTENANCE-FREE, FULLY SHIELDED, DEADFRONT AND SUBMERSIBLE.
 5. LOADBREAK JUNCTIONS AND CONNECTORS SHALL BE RATED FOR 200A CONTINUOUS, 10KA SYM., 10 CYCLES, 15KV CLASS, 95KV BIL.
 6. DEADBREAK JUNCTIONS AND CONNECTORS SHALL BE RATED FOR 600A CONTINUOUS, 25KA SYM., 10 CYCLES, 15/25KV CLASS, 140KV BIL.
 7. PROVIDE TEST POINT ON DEADBREAK AND LOADBREAK CONNECTORS.
 8. INSTALLATION PER MANUFACTURER'S RECOMMENDATION.

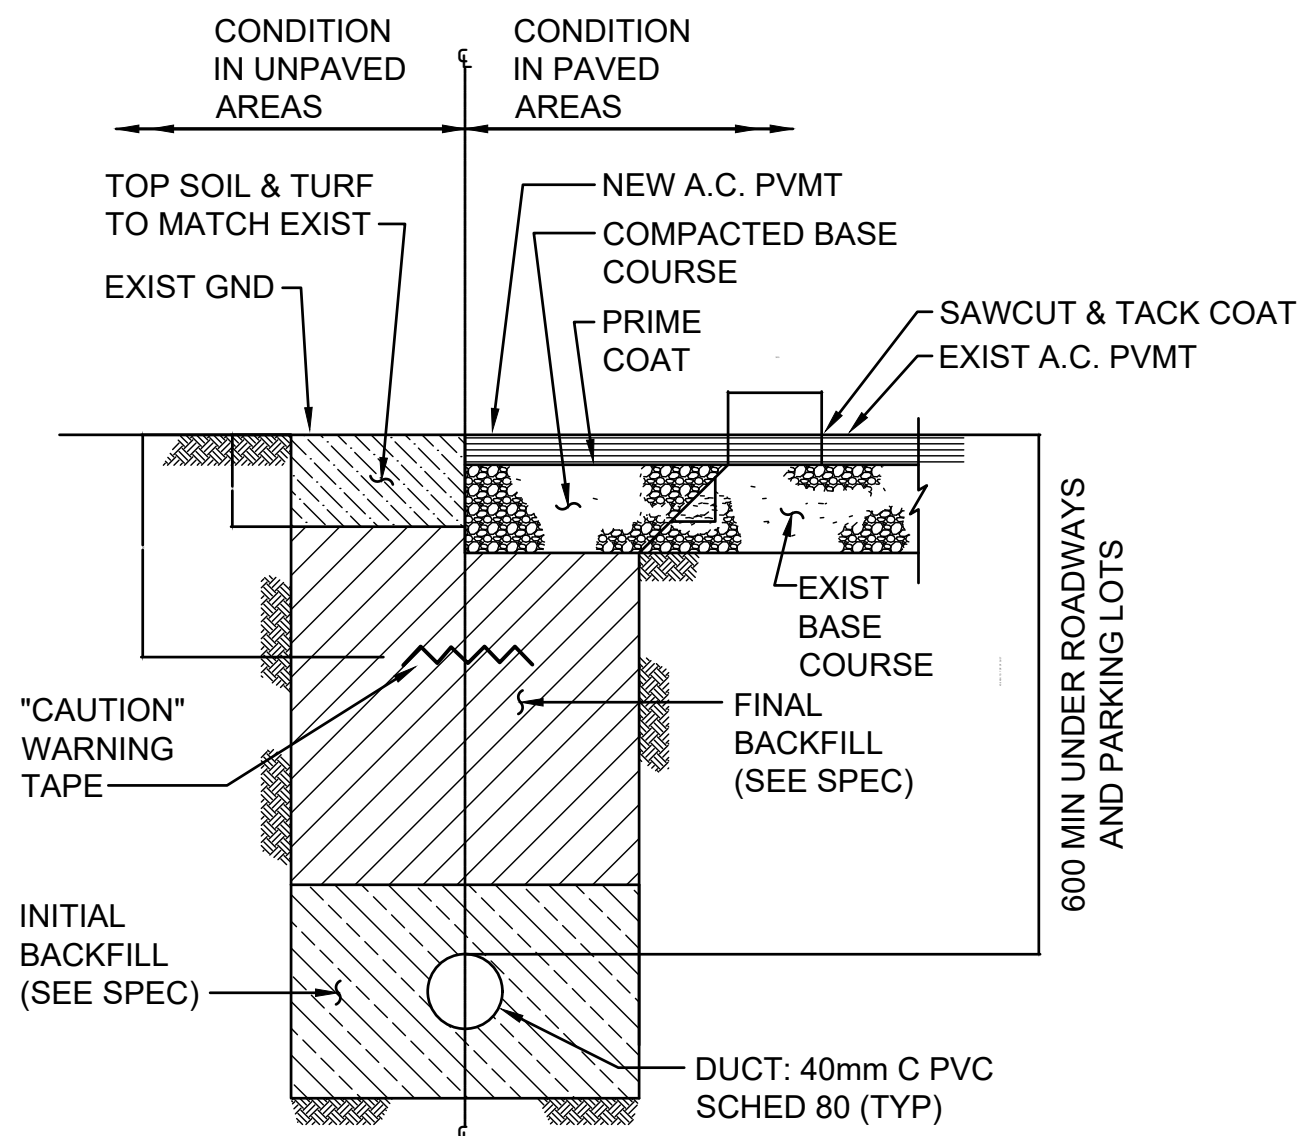


NOTE:

SEE SHEET ES501 FOR ADDITIONAL DETAILS.


K3 SITE LIGHTING DUCT SECTION

NONE

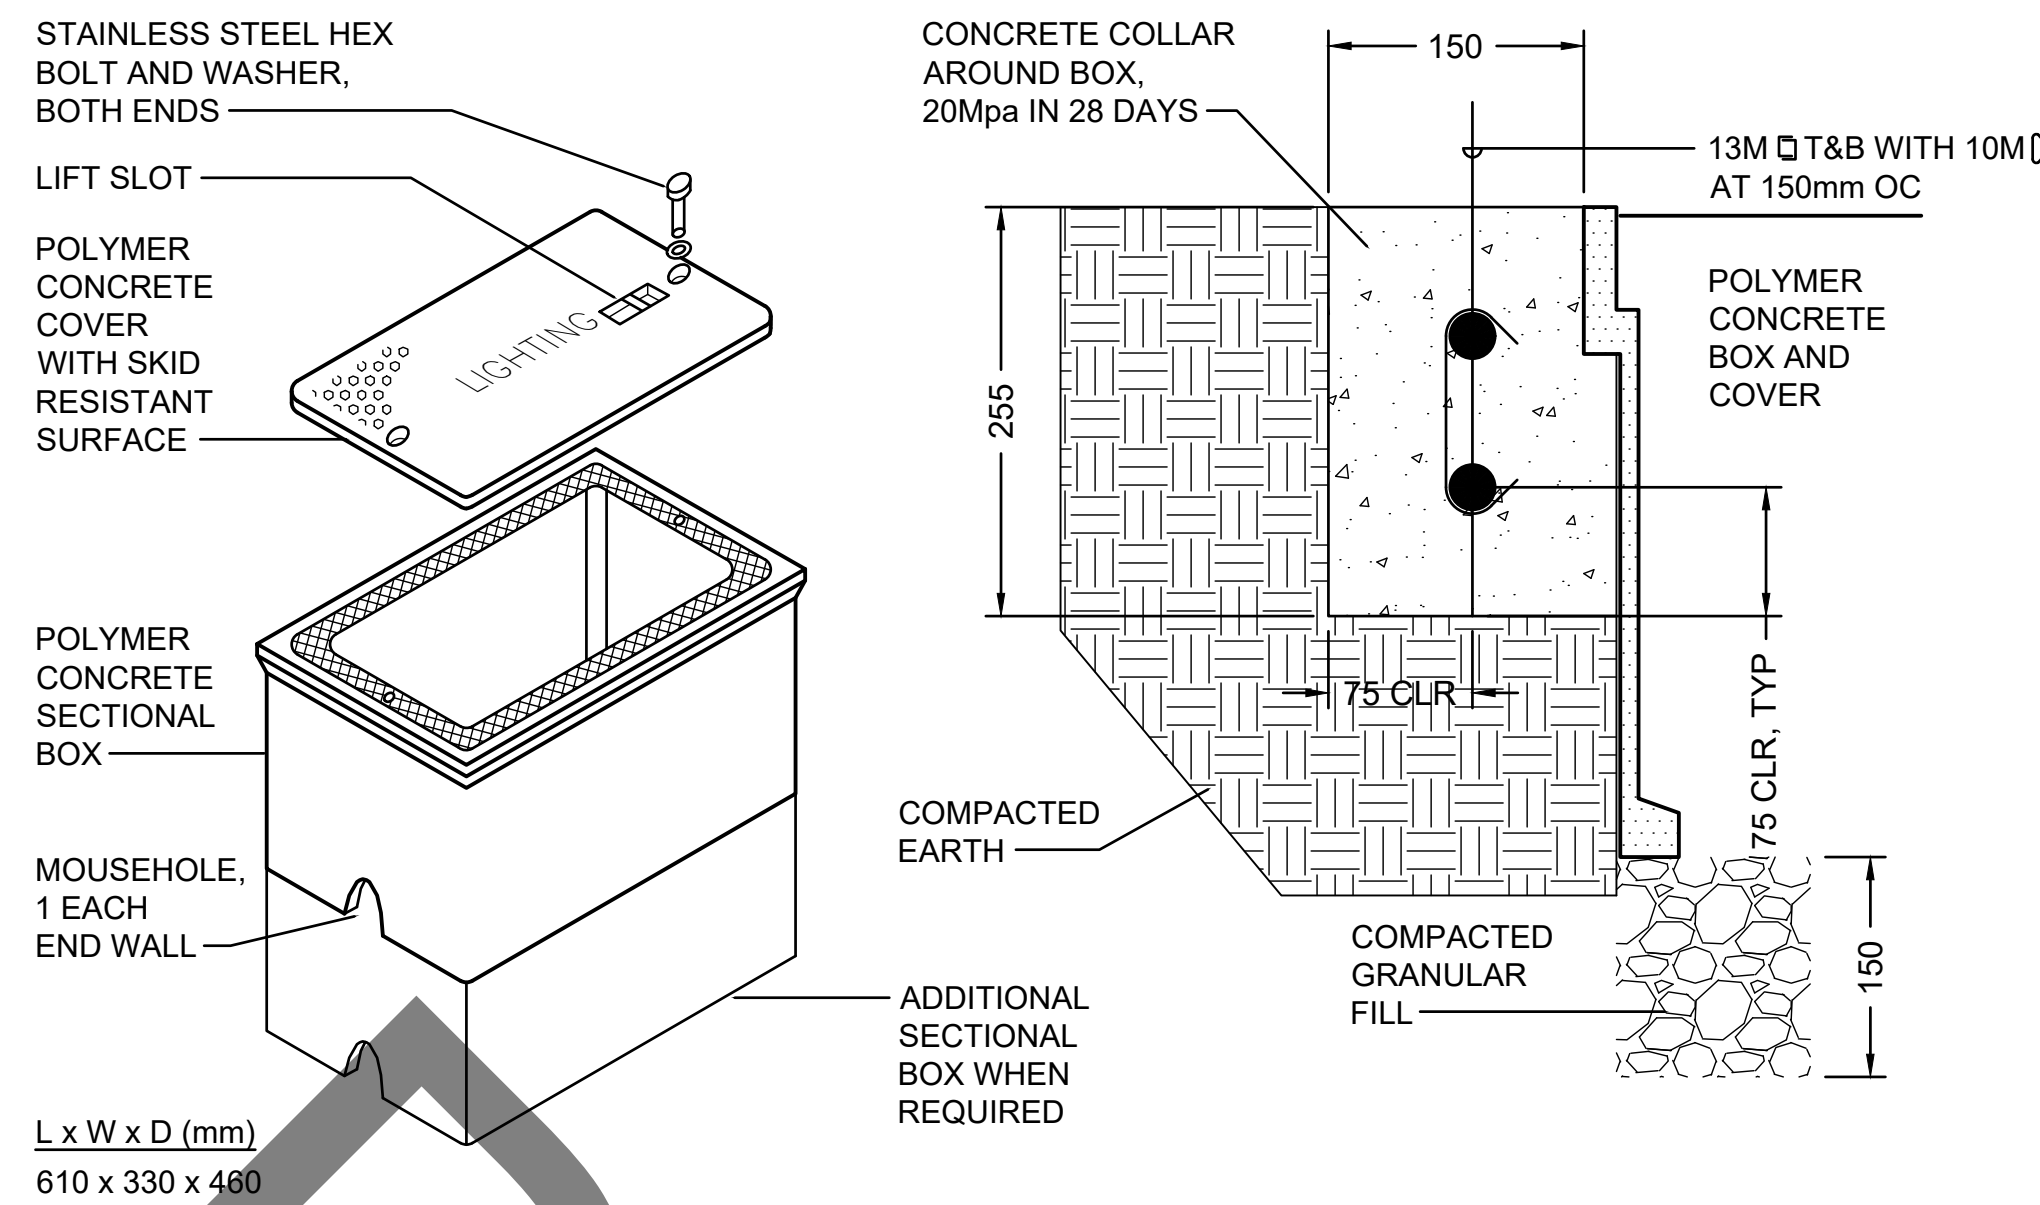

SITE LIGHTING PULLBOX DETAILS


NON

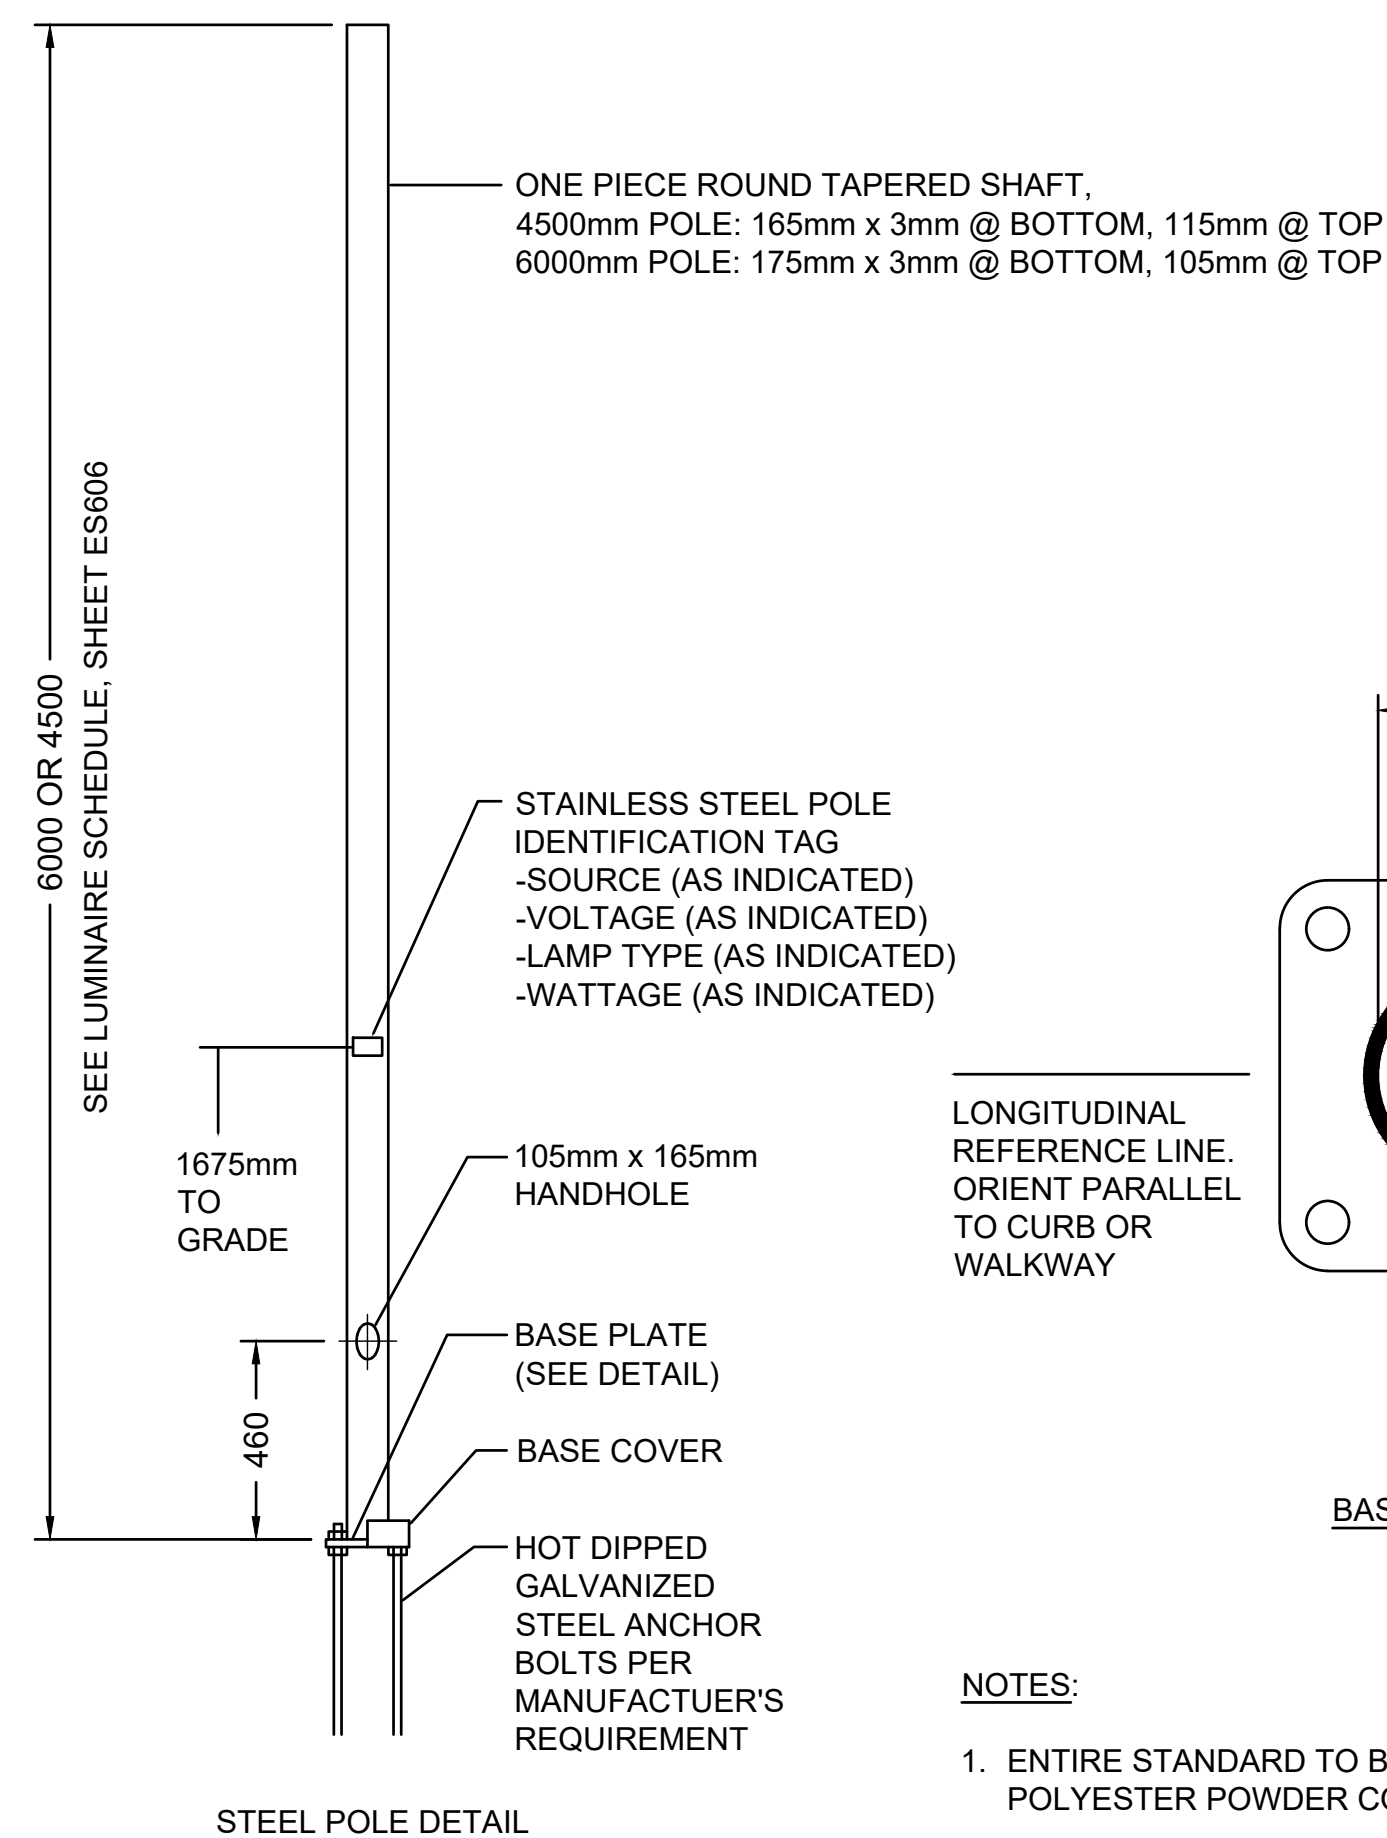


STEEL POLE DETAIL

NOTES:


1. ENTIRE STANDARD TO BE COATED WITH A THERMOSET POLYESTER POWDER COATING. COLOR TO MATCH FIXTURE.
2. POLES SHALL MEET THE REQUIREMENTS OF AASHTO LTS-5, 290km/hr WIND LOADING.

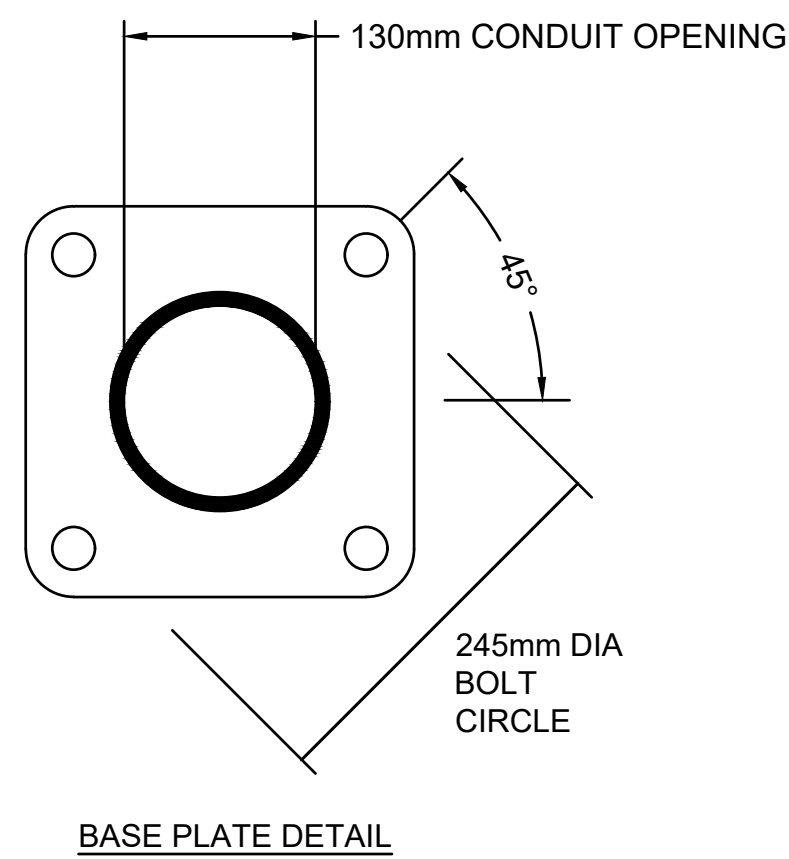

BASE PLATE DETAIL

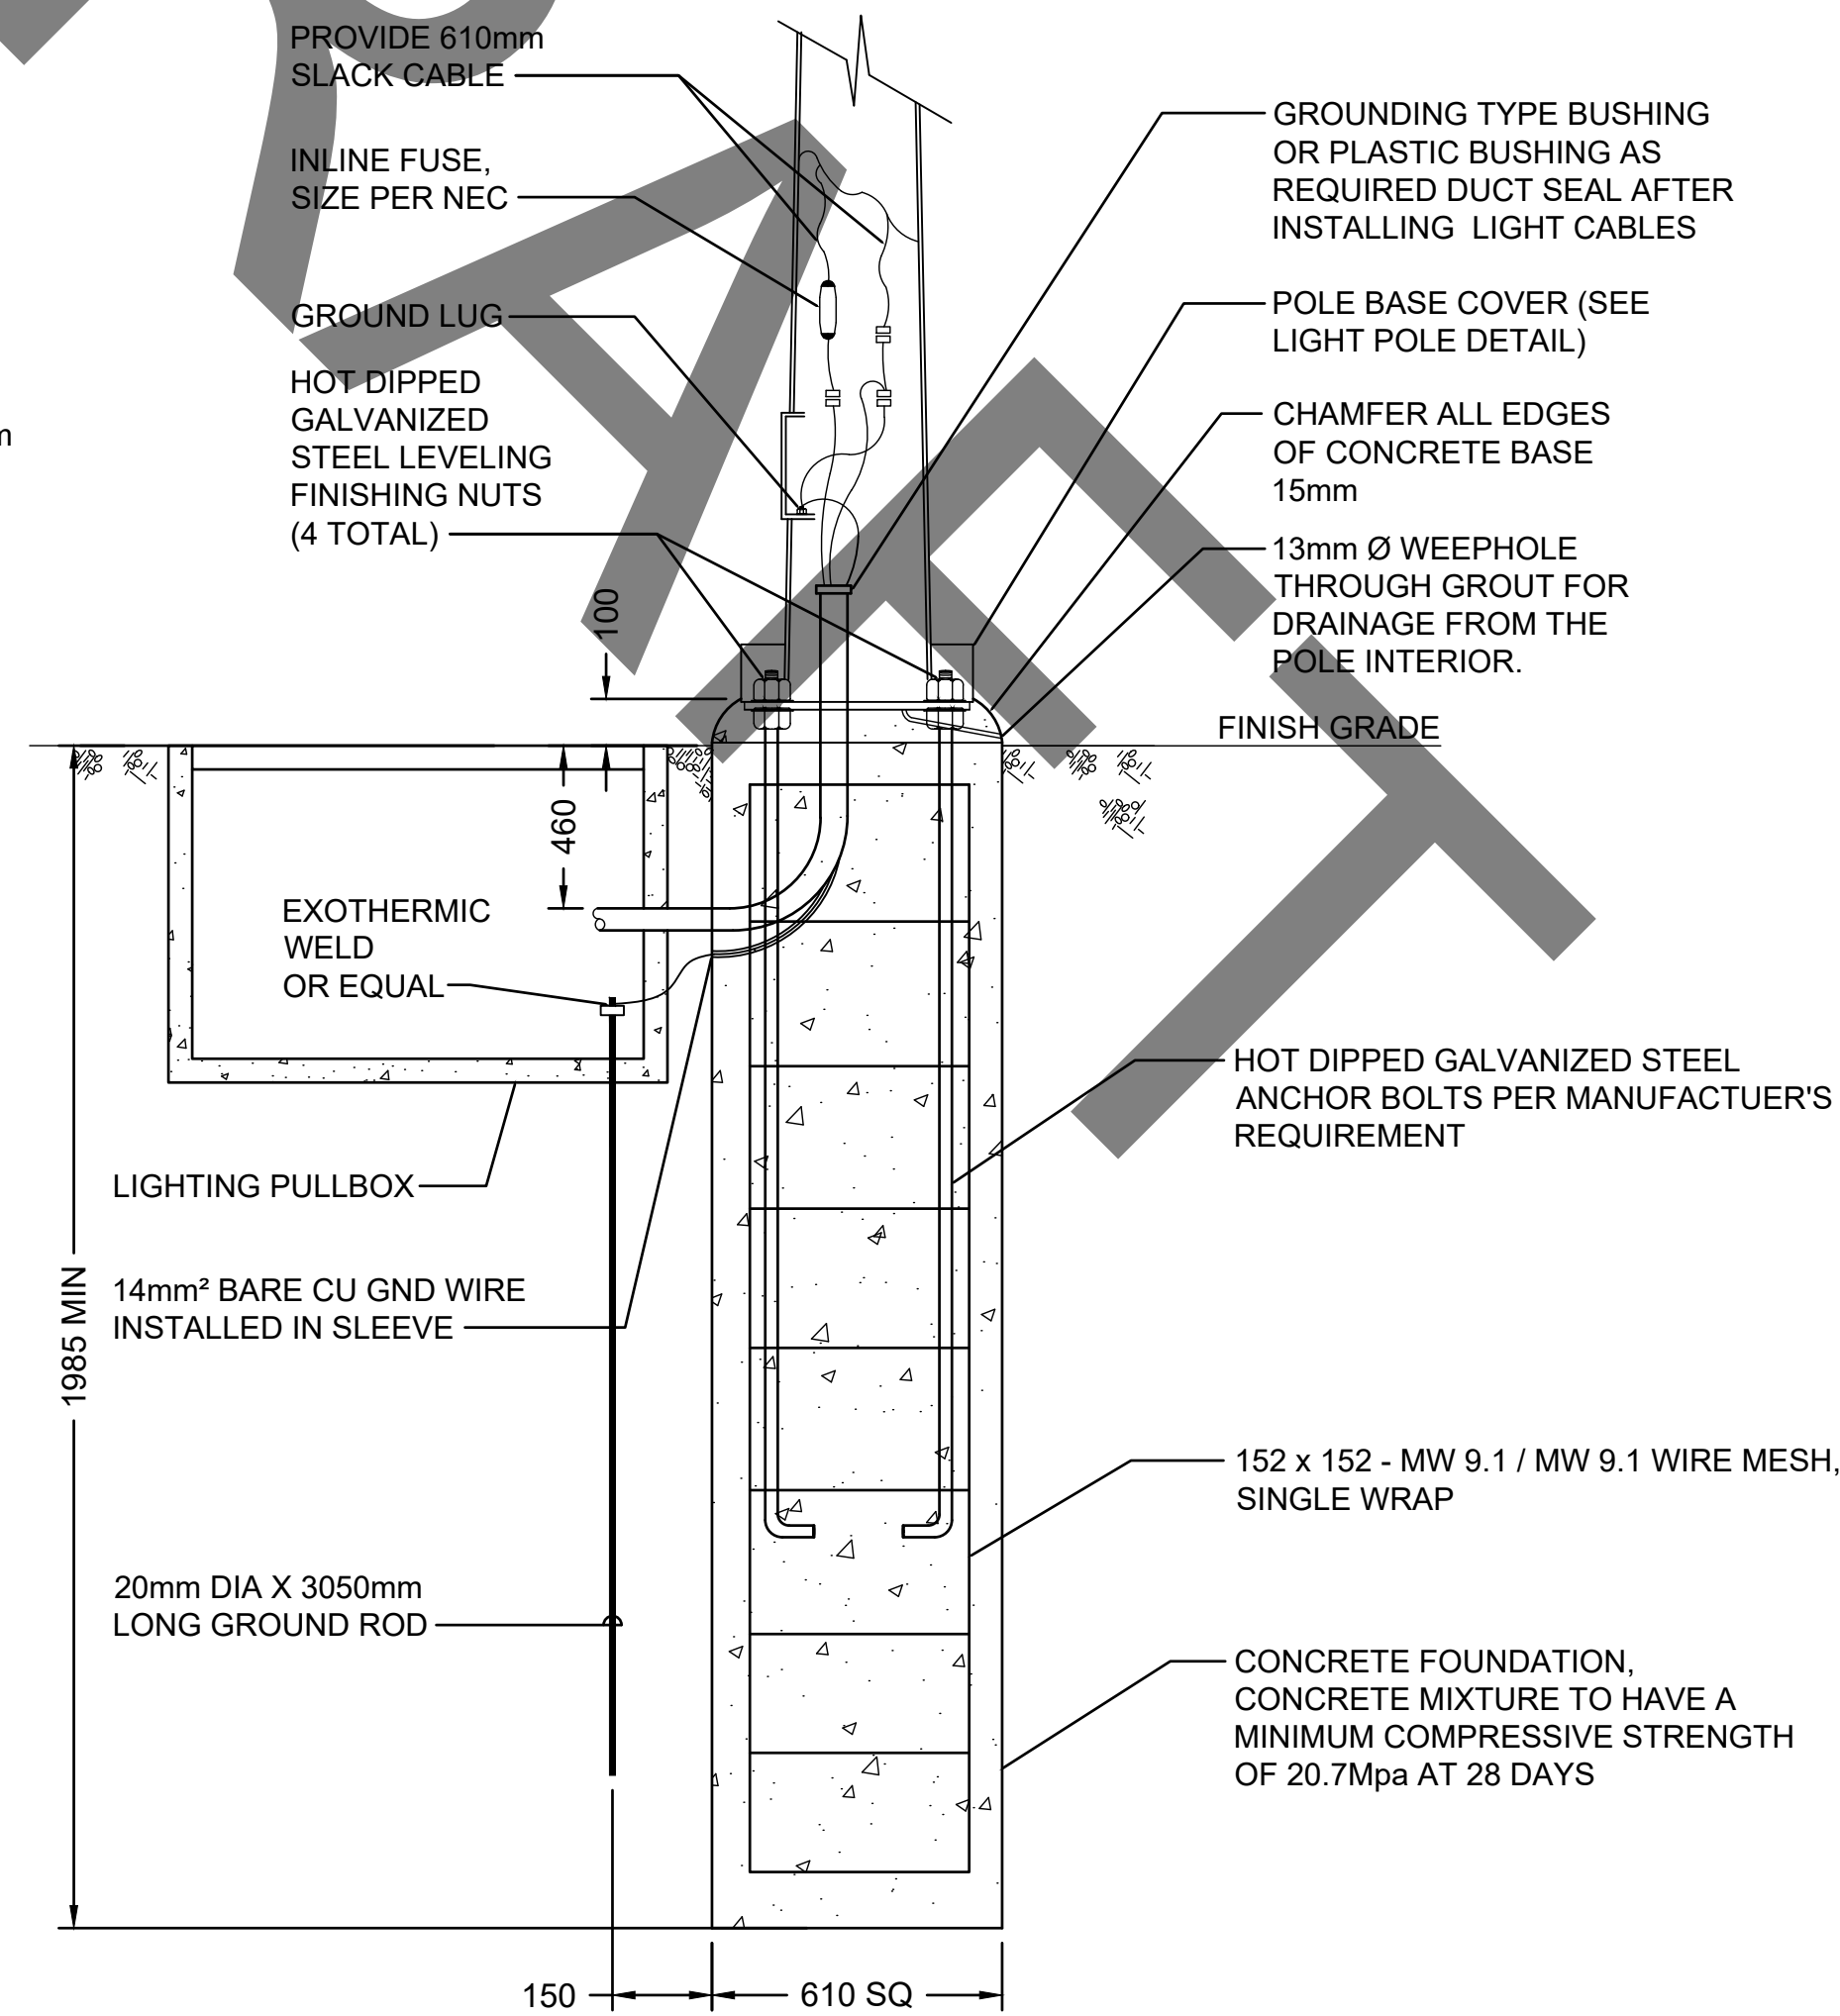

ANCHOR BASE DETAIL
APPLIES TO POLES LOCATED IN
GRASSED CLEAR ZONE AREA

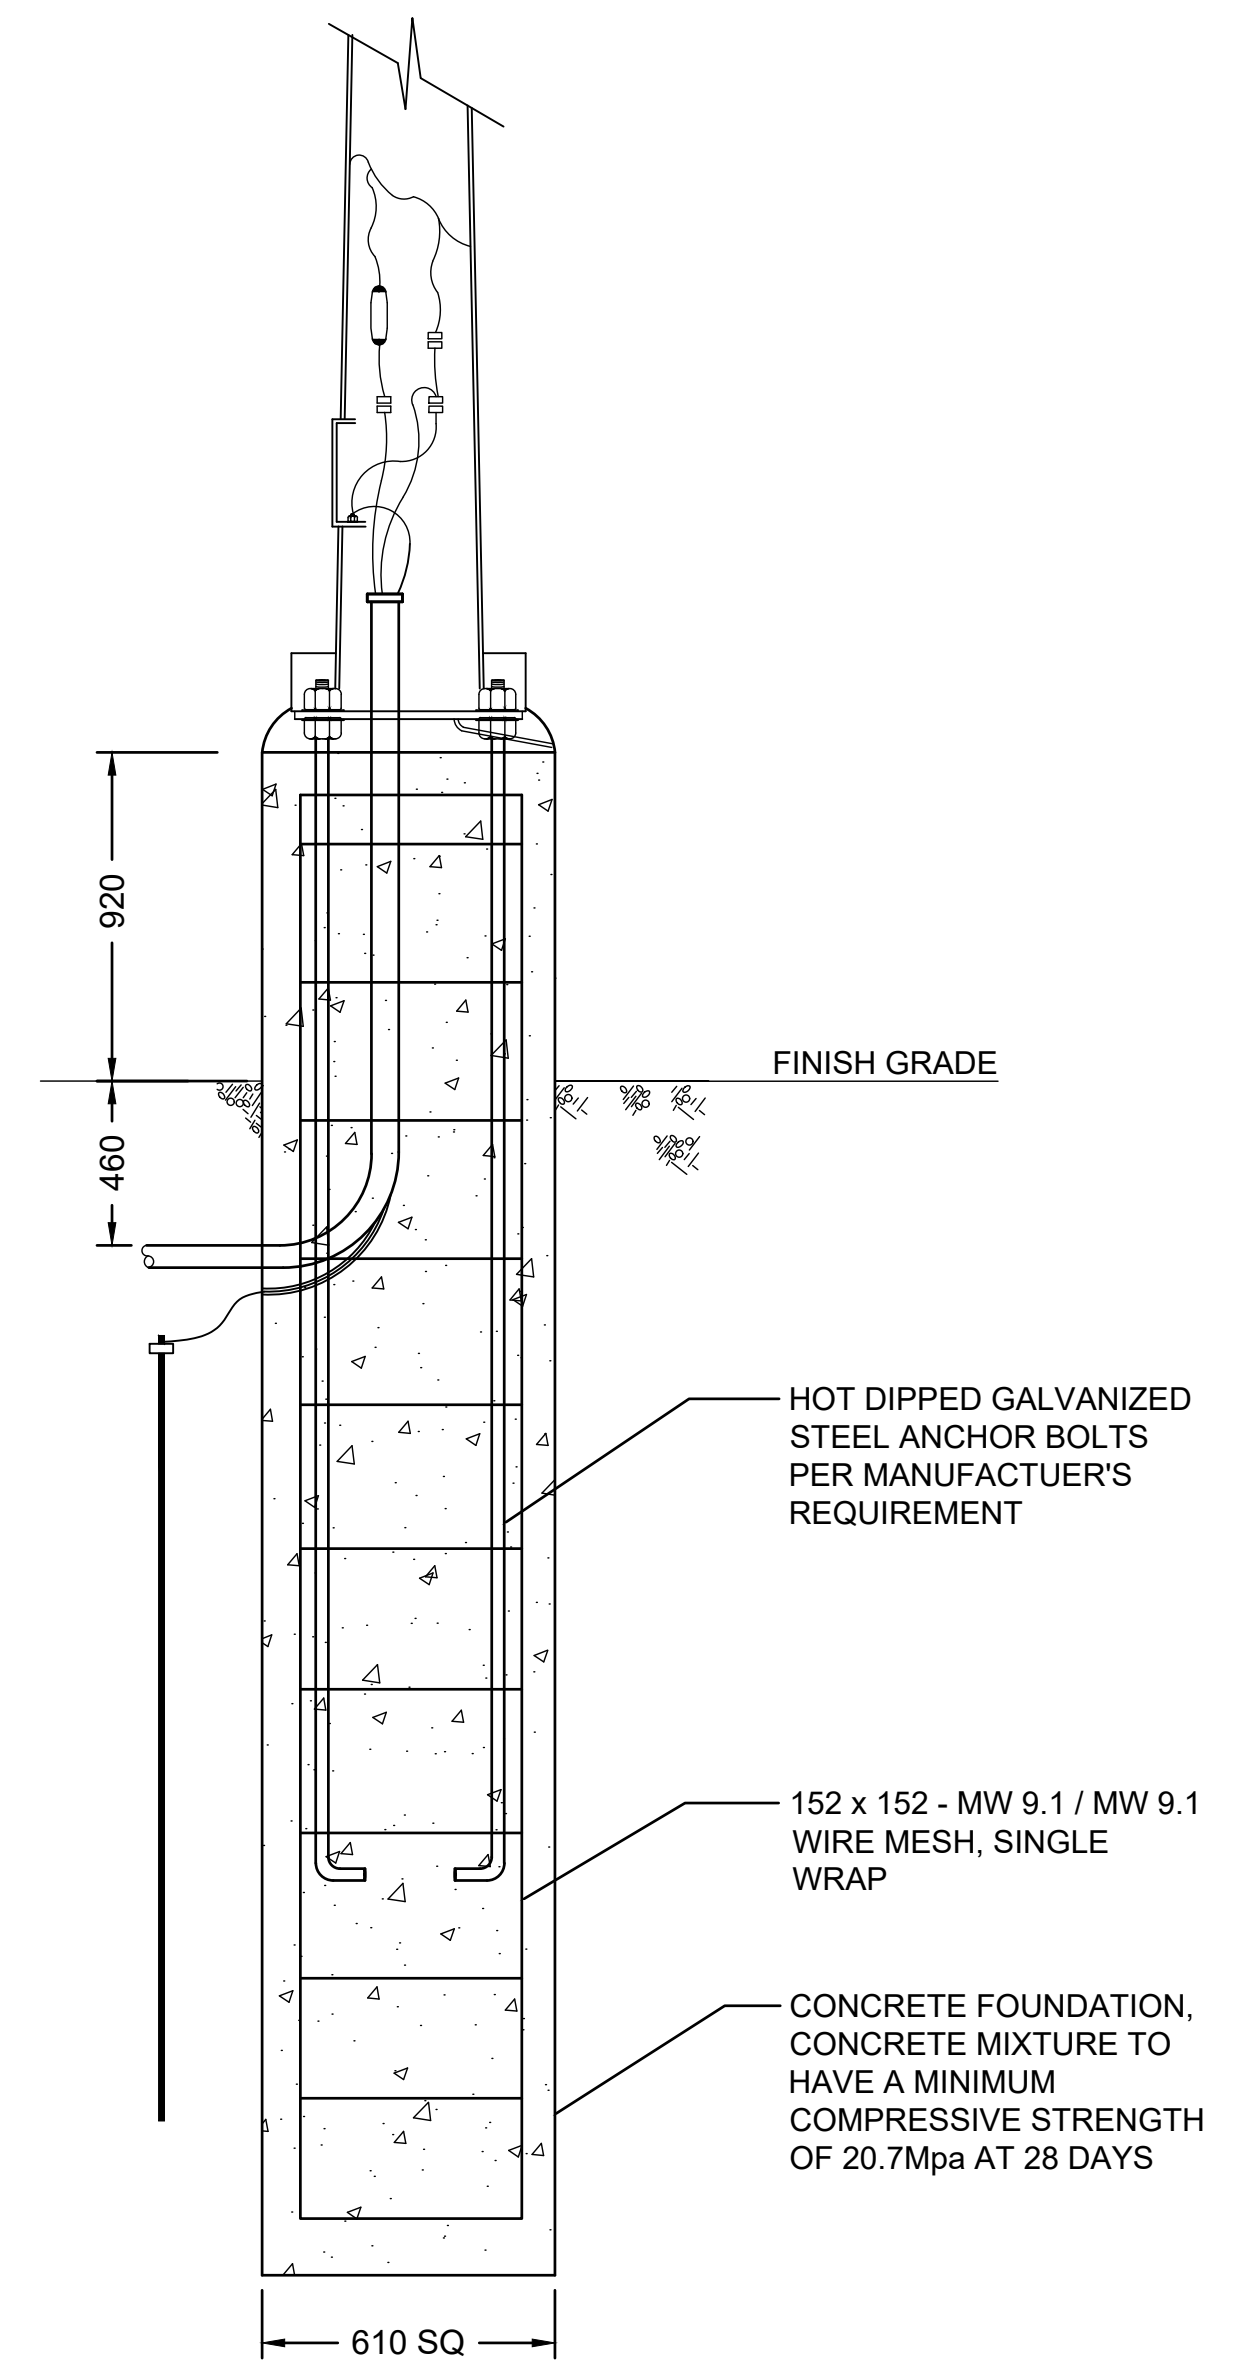

ANCHOR BASE DETAIL
APPLIES TO POLES LOCATED IN
THE MIDDLE OF PARKING LOT

JAPAN DISTRICT, OKINAWA AREA OFFICE		SOLICITATION NO.:	
USED-J UNIT 35132		CONTRACT NO.:	
APO, AP 96374-5132		SUBMITTED BY:	
SSM International, Inc.		AS SHOWN	
SSM INTERNATIONAL, INC.		FILE NAME:	
50 KALANANUOULI DRIVE #20		SIZE:	
HONOLULU, HAWAII 96817		ISO A1	

SITE LIGHTING DETAILS

SHEET ID

ES505

- SITE PREPARATION WORK FOR VMS FACILITIES.
- LOONEY STREET AND ELECTRICAL AND TELECOMMUNICATIONS INFRASTRUCTURE IMPROVEMENTS.
- CONSTRUCTION OF FIRE PUMP BUILDING, WATER STORAGE TANK, AND CABLE HUT.
- ENSURE THAT ELECTRICAL SERVICES TO EXISTING ADA BUILDINGS (B4040 THRU B4047) ARE MAINTAINED.
- RELOCATED JCP-871 AND ASSOCIATED ELECTRICAL EQUIPMENT AND DISTRIBUTION SYSTEMS TO ACCOMMODATE NEW PARKING LOT AND ACCESS ROAD TO K-SITES.
- CONSTRUCTION OF VEHICLE MAINTENANCE SHOP AND ASSOCIATED ELECTRICAL INFRASTRUCTURE.


- CONSTRUCTION OF ORGANIZATIONAL EQUIPMENT STORAGE, POL STORAGE, AND ASSOCIATED ELECTRICAL INFRASTRUCTURE.

- CONSTRUCTION OF ORGANIZATIONAL VEHICLE PARKING LOT.
- CONSTRUCTION OF WASH RACK.

- CONSTRUCTION OF TEMPORARY FACILITIES AT SWING SPACE SITE MUST BE COMPLETED PRIOR TO DEMOLITION OF EXISTING ADA BUILDINGS (B4040 THRU B4047) AND SITE PREPARATION WORK FOR SSA FACILITIES.
- CONSTRUCTION OF NEW SUPPLY SUPPORT ACTIVITY (SSA) WAREHOUSE, STORAGE SHED AND ASSOCIATED ELECTRICAL INFRASTRUCTURE.
- CONSTRUCTION OF SSA PARKING LOT.

1. UNDER CLING 0001 THRU 0003, EXISTING SERVICES TO ADA BUILDINGS SHALL BE MAINTAINED WHILE THE CRITICAL FIBER AND COPPER CABLES IN BLDG 4040 WILL BE RELOCATED TO THE NEW CABLE HUT.
2. NEW FACILITIES AT SWING SPACE SHALL BE ESTABLISHED PRIOR TO DEMOLITION OF ADA BUILDINGS UNDER CLIN 0004.

- 1 EXISTING MANHOLE AND ASSOCIATED INFRASTRUCTURE AND FEEDER CONDUCTORS TO REMAIN SHALL BE PROTECTED DURING THE GRADING WORK.
- 2 EXISTING CJP's AND TRANSFORMERS TO REMAIN AND THE FACILITIES THAT ARE SERVED BY THESE EQUIPMENT SHALL REMAIN OPERATIONAL.
- 3 EXISTING CJP's AND ASSOCIATED FEEDER CONDUCTORS SHALL BE REMOVED. COORDINATE AND PHASE THE REMOVAL AND NEW WORK TO MINIMIZE SERVICE OUTAGES.
- 4 EXISTING CJP's, TRANSFORMERS, AND ASSOCIATED PRIMARY & SECONDARY FEEDER CONDUCTORS, AND DISTRIBUTION EQUIPMENT SERVING ADA BUILDINGS SHALL REMAIN IN SERVICE UNDER CLIN 0001-0003. THEY WILL BE DEMOLISHED UNDER CLIN 0004.
- 5 EXISTING CJP, TRANSFORMER, INFRASTRUCTURE, AND FEEDER CONDUCTORS SERVING B4049 (SEWAGE LIFT STATION) SHALL REMAIN IN SERVICE. THE PRIMARY FEEDER TO B4049 WILL BE SWITCHED TO CIRCUIT T3 TO MAINTAIN ITS OPERATION WHEN CIRCUIT T1 IS NOT AVAILABLE. COORDINATE THE WORK WITH THE BASE UTILITY.
- 6 EXISTING INFRASTRUCTURE, OH TRANSFORMER, AND SECONDARY OH FEEDER CONDUCTORS SERVING THE RECYCLING CENTER YARD SHALL SALVAGED AND RE-CONNECTION TO THE NEW FEEDER.
- 7 THE EXISTING PRIMARY FEEDER CONDUCTORS SHALL BE SALVAGED AND PROTECTED FOR SPlicing TO A NEW FEEDER CIRCUIT.

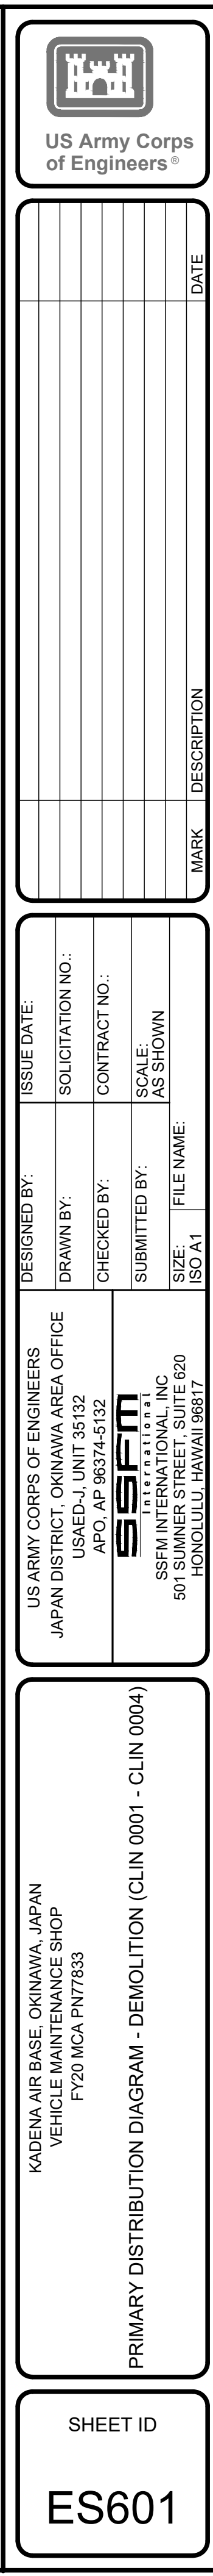

P
—
O
—
N
—
M
—
L
—
K
—
J
—
I
—
H
—
G
—
F
—
E
—
D
—
C
—
B
—
A

A — B — C — D — E — F — G — H — I — J — K — L — M — N — O

- A — B — C — D — E — F — G — H — I — J — K — L —



US Army Corps
of Engineers®

- [illegible]

KADENA AIR BASE, OKINAWA, JAPAN
VEHICLE MAINTENANCE SHOP
FY20 MCA PN177833

INTERMEDIATE DESIGN

- CONSTRUCTION OF ORGANIZATIONAL VEHICLE PARKING LOT.
- CONSTRUCTION OF WASH RACK.

- CONSTRUCTION OF TEMPORARY FACILITIES AT SWING SPACE SITE MUST BE COMPLETED PRIOR TO DEMOLITION OF EXISTING ADA BUILDINGS (B4040 THRU B4047) AND SITE PREPARATION WORK FOR SSA FACILITIES.
- CONSTRUCTION OF NEW SUPPLY SUPPORT ACTIVITY (SSA) WAREHOUSE, STORAGE SHED AND ASSOCIATED ELECTRICAL INFRASTRUCTURE.
- CONSTRUCTION OF SSA PARKING LOT.

1 EXTEND A NEW FEEDER TO THE TRANSFORMER SERVING THE
SSAW BUILDING FROM CJP-03.



JAPAN DISTRICT, OKINAWA AREA OFFICE	
USAED-J UNIT 35132	
APO, AP 96374-5132	
	
SSPM INTERNATIONAL, INC.	
501 KALANIANA'OLUHIA DRIVE, #20	
HONOLULU, HAWAII 96817	
DRAWN BY:	SOLICITATION NO.:
CHECKED BY:	CONTRACT NO.:
SUBMITTED BY:	SCALE:
SIZE:	FILE NAME:
ISO A1	

ES621

INTERMEDIATE DESIGN

- CONSTRUCTION OF TEMPORARY FACILITIES AT SWING SPACE SITE MUST BE COMPLETED PRIOR TO DEMOLITION OF EXISTING ADA BUILDINGS (B4040 THRU B4047) AND SITE PREPARATION WORK FOR SSA FACILITIES.
- CONSTRUCTION OF NEW SUPPLY SUPPORT ACTIVITY (SSA) WAREHOUSE, STORAGE SHED AND ASSOCIATED ELECTRICAL INFRASTRUCTURE.
- CONSTRUCTION OF SSA PARKING LOT.



1. EXTEND A NEW FEEDER TO THE TRANSFORMER SERVING THE COF BUILDING AND ARMORY FROM EXISTING CJP.
2. EXISTING SERVICE TO BLDG 4048 SHALL BE PROTECTED AND REMAIN IN SERVICE.

[illegible]

JAPAN DISTRICT, OKINAWA AREA OFFICE		SOLICITATION NO.:	
USAED-4, UNIT 35132		DRAWN BY:	
APO, AP 96374-5132		CHECKED BY:	
 SSPM INTERNATIONAL, INC. 501 KALANANU'U DRIVE, #20 HONOLULU, HAWAII 96817		CONTRACT NO.:	
		SCALE: AS SHOWN	
		SUBMITTED BY:	
SIZE: FILE NAME: ISO A1			

MADEIRA AIR BASE, OKINAWA, JAPAN
VEHICLE MAINTENANCE SHOP
FY20 MCA PN77833


SHEET ID

ES631

INTERMEDIATE DESIGN

A — B — C — D — E — F — G — H — I — J — K — L — M — N — O — P

P
O
N
M
L
K
J
I
H
G
F
E
D
C
B
A

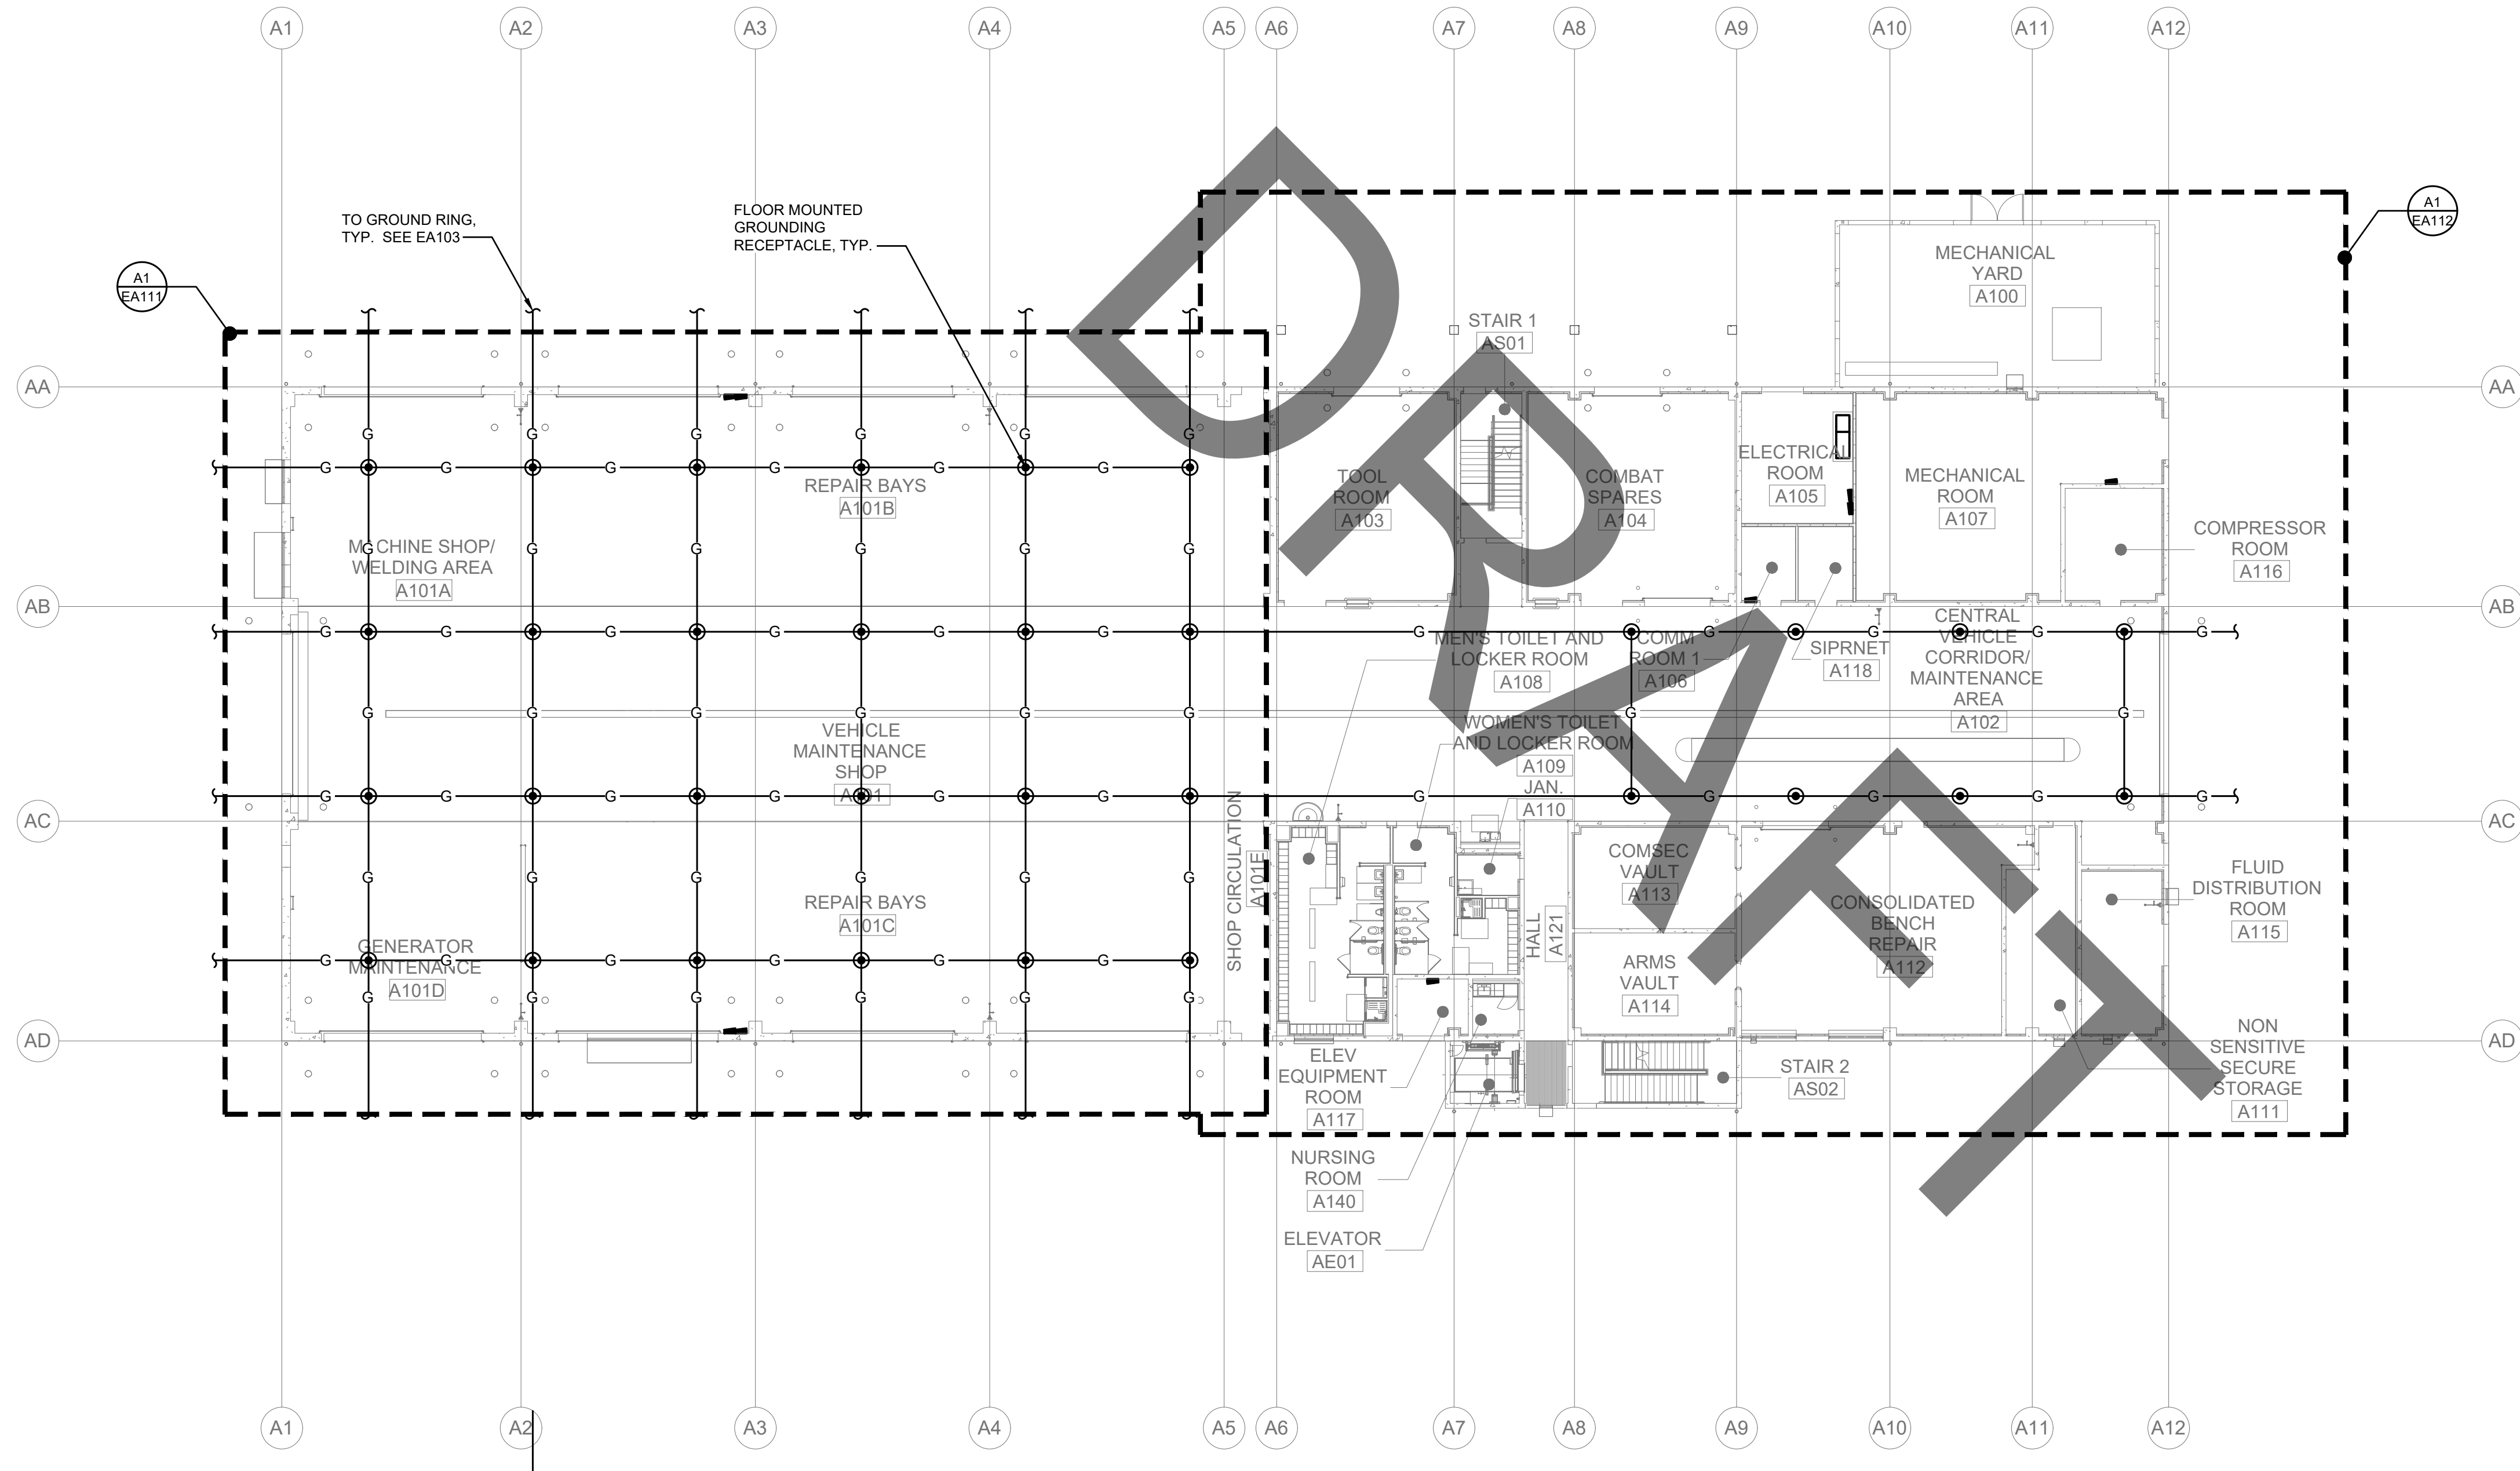

A1 VMS - OVERALL FIRST FLOOR PLAN (CLIN 0001)

GENERAL NOTES




US Army Corps
of Engineers®

LEGEND

CLIN 0001


KEY PLAN

VMS - LEVEL 1
N.T.S.

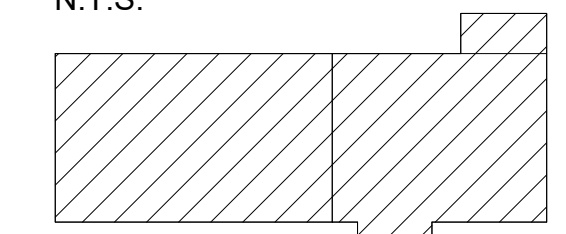

GRAPHIC SCALE


PLAN
NORTH

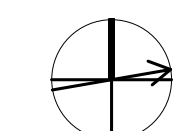

SCALE: 1 : 200



ALL DIMENSIONS AND/OR DIMENSIONS SHOWN IN
CALLOUT/NOTES ARE IN MILLIMETERS UNLESS
OTHERWISE NOTED.

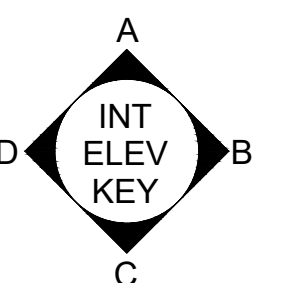

US ARMY CORPS OF ENGINEERS
JAPAN DISTRICT, OKINAWA AREA OFFICE
USAED-J UNIT 35132
APO, AP 96374-5132

DESIGNED BY:
DRAWN BY:
CHECKED BY:
SUBMITTED BY:
SIZE: ISO A1
FILE NAME:

ISSUE DATE:
SOLICITATION NO.:
CONTRACT NO.:
SCALE: AS SHOWN


SSFM
SSFM INTERNATIONAL, INC.
501 SUMNER STREET, SUITE 620
HONOLULU, HAWAII 96817

KADENA AIR BASE, OKINAWA, JAPAN
VEHICLE MAINTENANCE SHOP
FY20 MCA PN77833
VMS - OVERALL FIRST FLOOR PLAN (CLIN 0001)

SHEET ID

EA101

INTERMEDIATE DESIGN

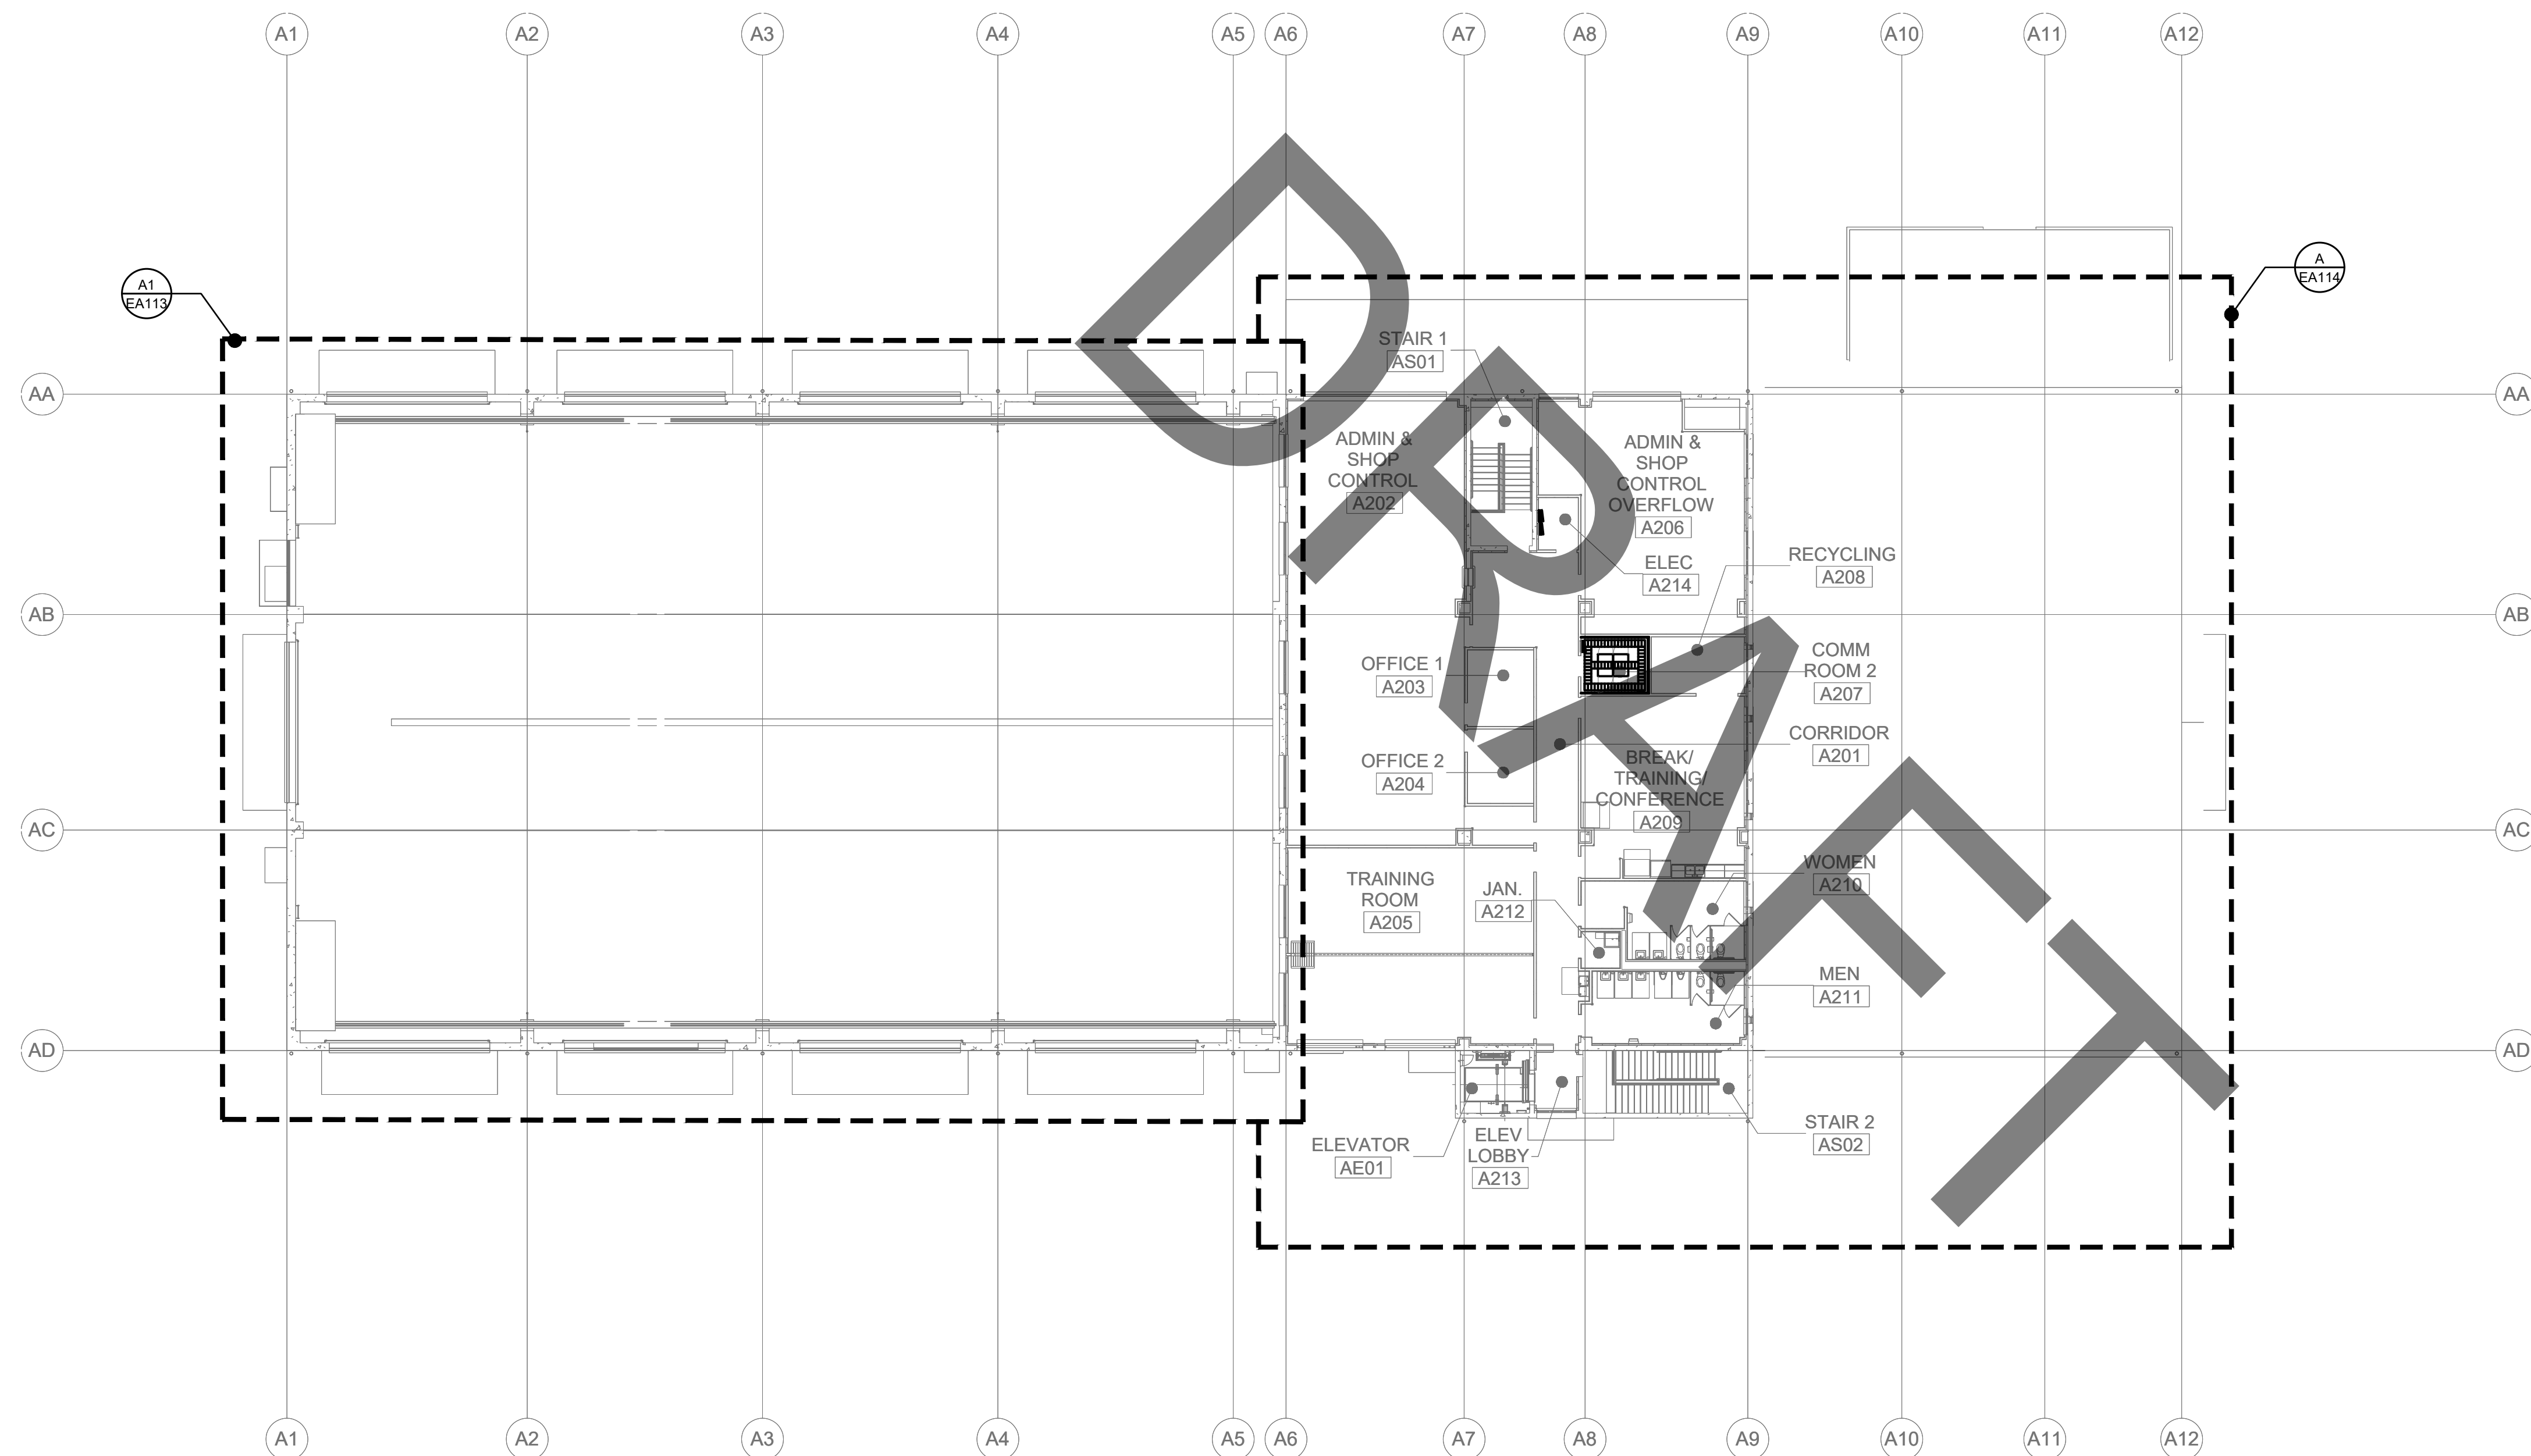

A1 VMS - OVERALL SECOND FLOOR PLAN (CLIN 0001)
1:200

GENERAL NOTES

US Army Corps
of Engineers®

Item	Value	Unit
1. 1000	1000	1000
2. 1000	1000	1000
LEGEND

SSPM INTERNATIONAL SSPM INTERNATIONAL, INC 501 SUMNER STREET, SUITE 620	DESIGNED BY:	ISSUE DATE:
	DRAWN BY:	SOLICITATION NO.:
	CHECKED BY:	CONTRACT NO.:
	SUBMITTED BY:	SCALE:
	SIZE:	FILE NAME:

KADENA AIR BASE, OKINAWA, JAPAN
VEHICLE MAINTENANCE SHOP
FY20 MCA PN77833

SHEET ID


EA102

INTERMEDIATE DESIGN


CLIN 0001

KEY PLAN


VMS - LEVEL 2
N.T.S.

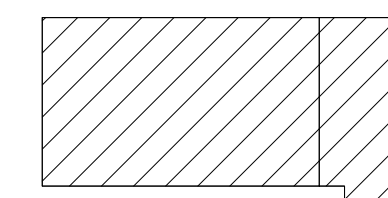

GRAPHIC SCALE

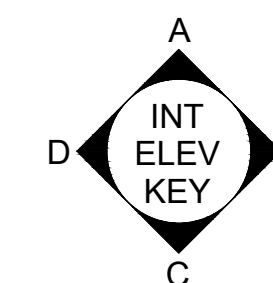


PLAN
NORTH

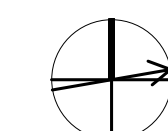

SCALE: 1 : 200



ALL DIMENSIONS AND/OR DIMENSIONS SHOWN IN
CALLOUT/ NOTES ARE IN MILLIMETERS UNLESS
OTHERWISE NOTED.

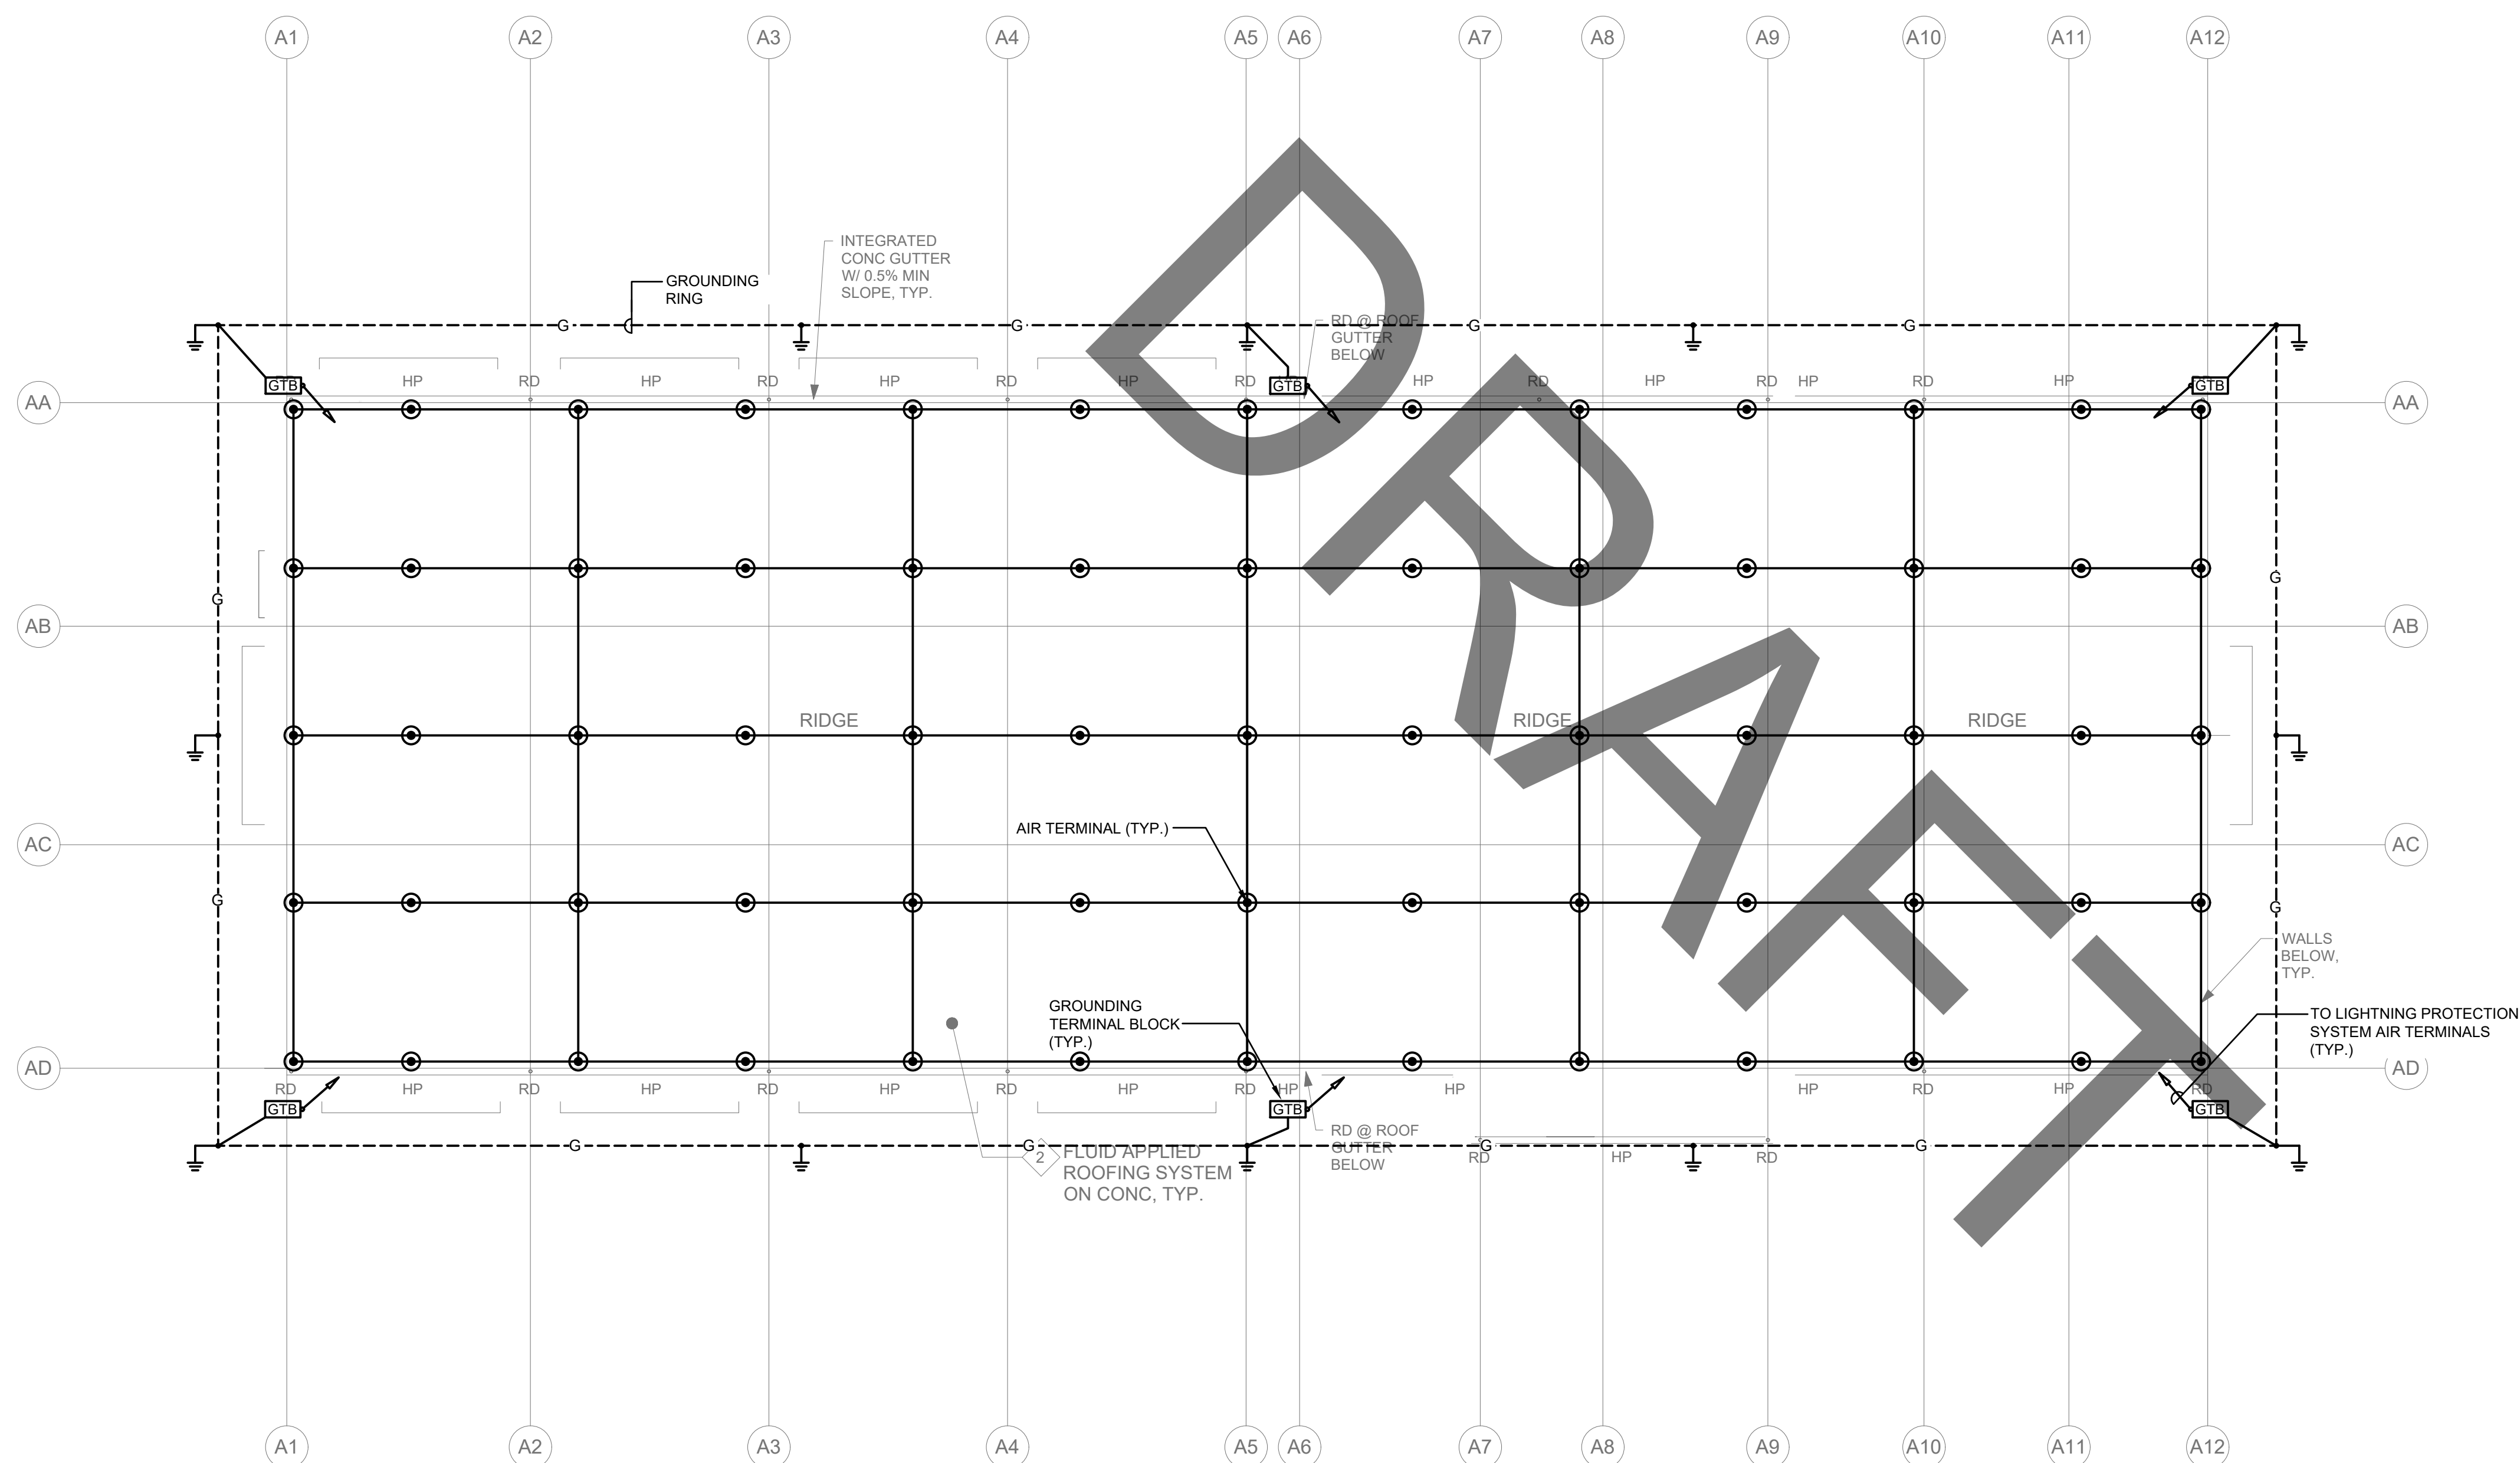


A1 VMS - LIGHTNING PROTECTION PLAN (CLIN 0001)
1:200

GENERAL NOTES

US Army Corps
of Engineers®[illegible]

LEGEND

 DESIGNED BY:	ISSUE DATE:
DRAWN BY:	SOLICITATION NO.:
CHECKED BY:	CONTRACT NO.:
SUBMITTED BY:	SCALE: AS SHOWN
	FILE NAME:
US ARMY CORPS OF ENGINEERS JAPAN DISTRICT, OKINAWA AREA OFFICE USAE-J UNIT 35132 APO, AP 96374-5132 SFSM INTERNATIONAL, INC. 551 SUMNER STREET, SUITE 620 FORT WORTH, TEXAS 76102	

KADENA AIR BASE, OKINAWA, JAPAN
VEHICLE MAINTENANCE SHOP
FY20 MCA PN77833

SHEET ID


EA103

INTERMEDIATE DESIGN

CLIN 0001

KEY PLAN


VMS - LEVEL 1
N.T.S.

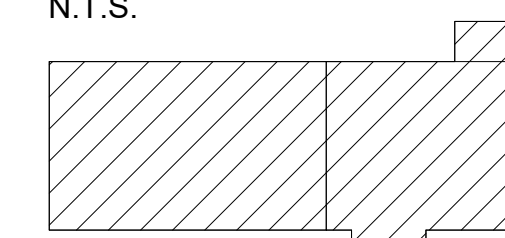


GRAPHIC SCALE




SCALE: 1 : 200

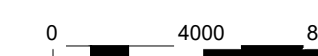

ALL DIMENSIONS AND/OR DIMENSIONS SHOWN IN
CALLOUT/ NOTES ARE IN MILLIMETERS UNLESS
OTHERWISE NOTED.

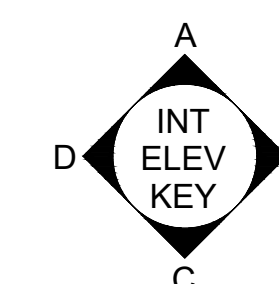

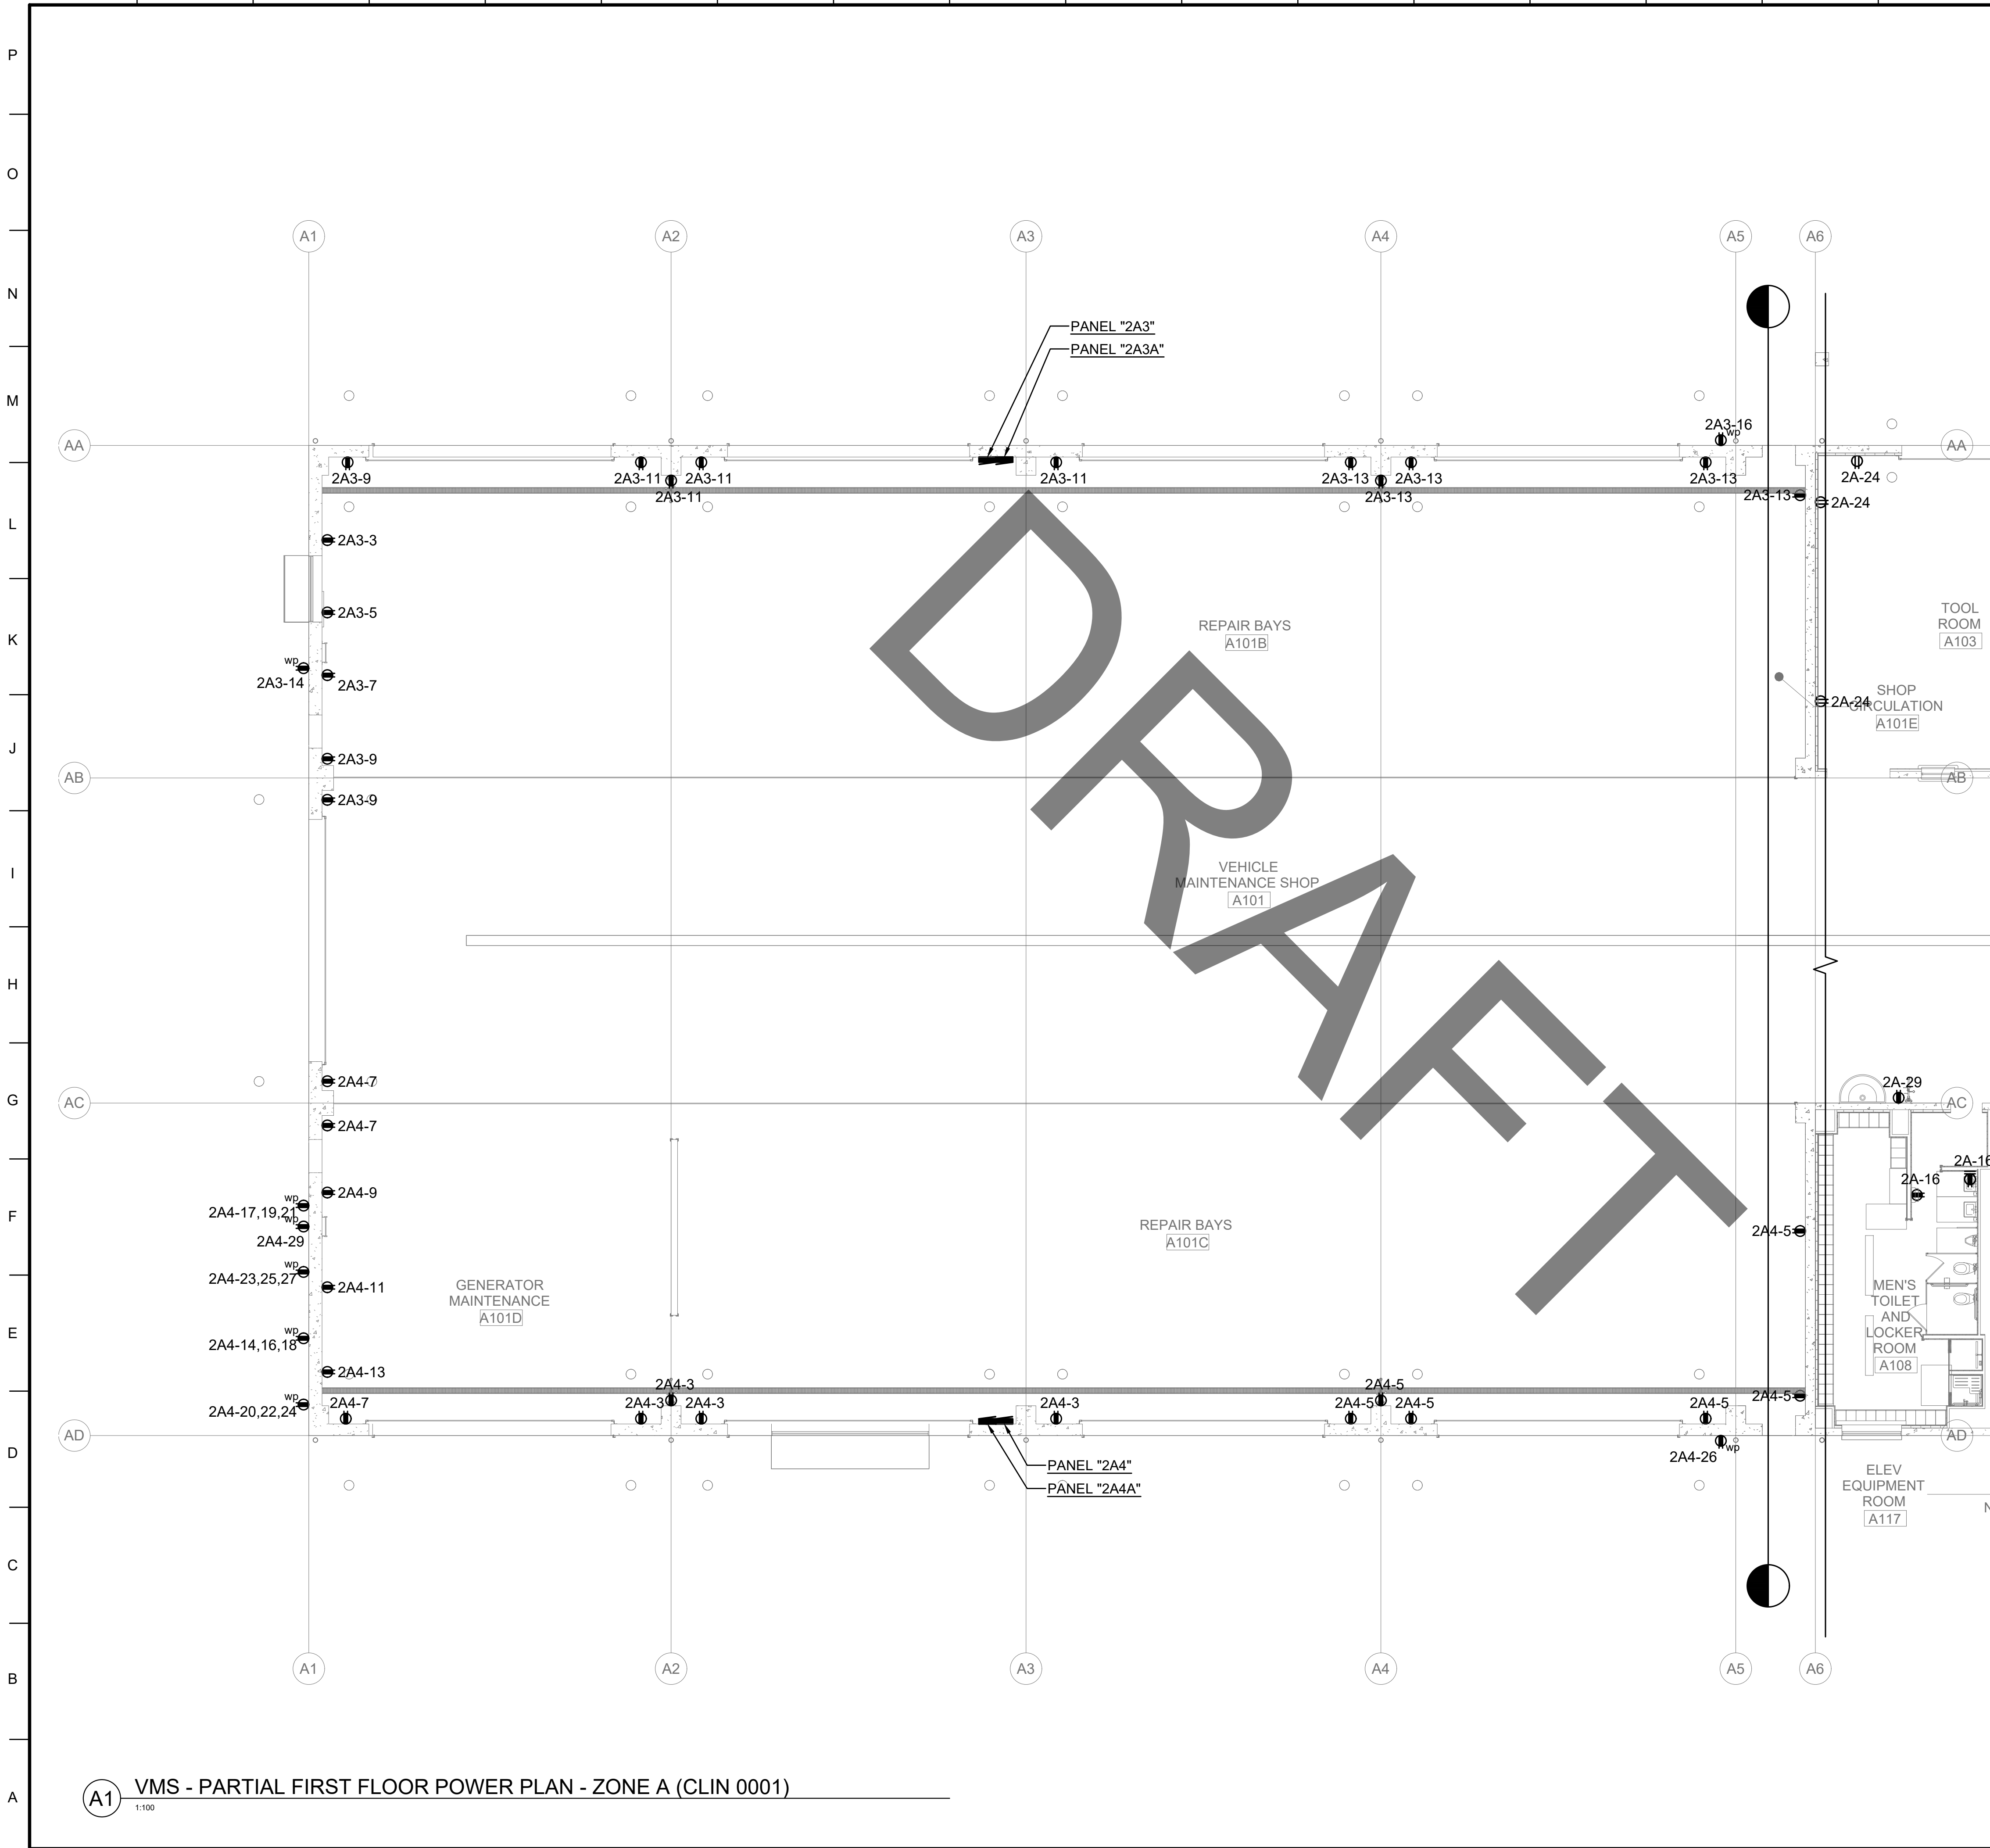


A1 VMS - PARTIAL FIRST FLOOR POWER PLAN - ZONE A (CLIN 0001)
1:100

GENERAL NOTES

LEGEND

CLIN 0001



KEY PLAN

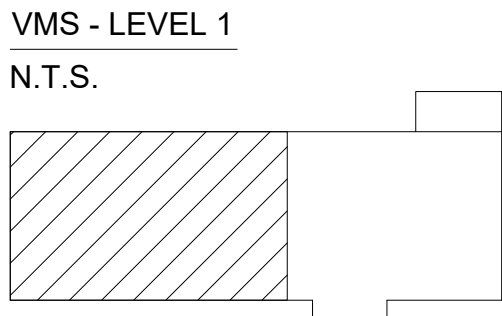

GRAPHIC SCALE



SCALE: 1 : 100
0 2000 4000
ALL DIMENSIONS AND/OR DIMENSIONS SHOWN IN CALLOUT/ NOTES ARE IN MILLIMETERS UNLESS OTHERWISE NOTED.

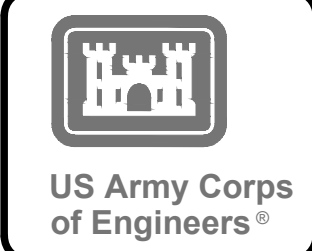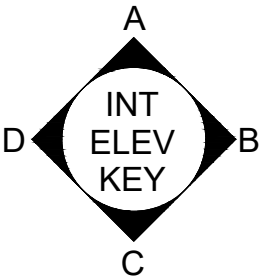


DATE	DESCRIPTION	MARK

DESIGNED BY:	ISSUE DATE:
DRAWN BY:	SOLICITATION NO.:
CHECKED BY:	CONTRACT NO.:
SUBMITTED BY:	SCALE:
FILE NAME:	AS SHOWN
ISO A1	
US ARMY CORPS OF ENGINEERS JAPAN DISTRICT, OKINAWA AREA OFFICE USAED-J UNIT 35132 APO, AP 96374-5132	SSFM SSFM INTERNATIONAL, INC. 501 SUMNER STREET, SUITE 620 HONOLULU, HAWAII 96817


KADENA AIR BASE, OKINAWA, JAPAN
VEHICLE MAINTENANCE SHOP
FY20 MCA PN77833
VMS - PARTIAL FIRST FLOOR POWER PLAN - ZONE A (CLIN 0001)

SHEET ID
EA111

INTERMEDIATE DESIGN

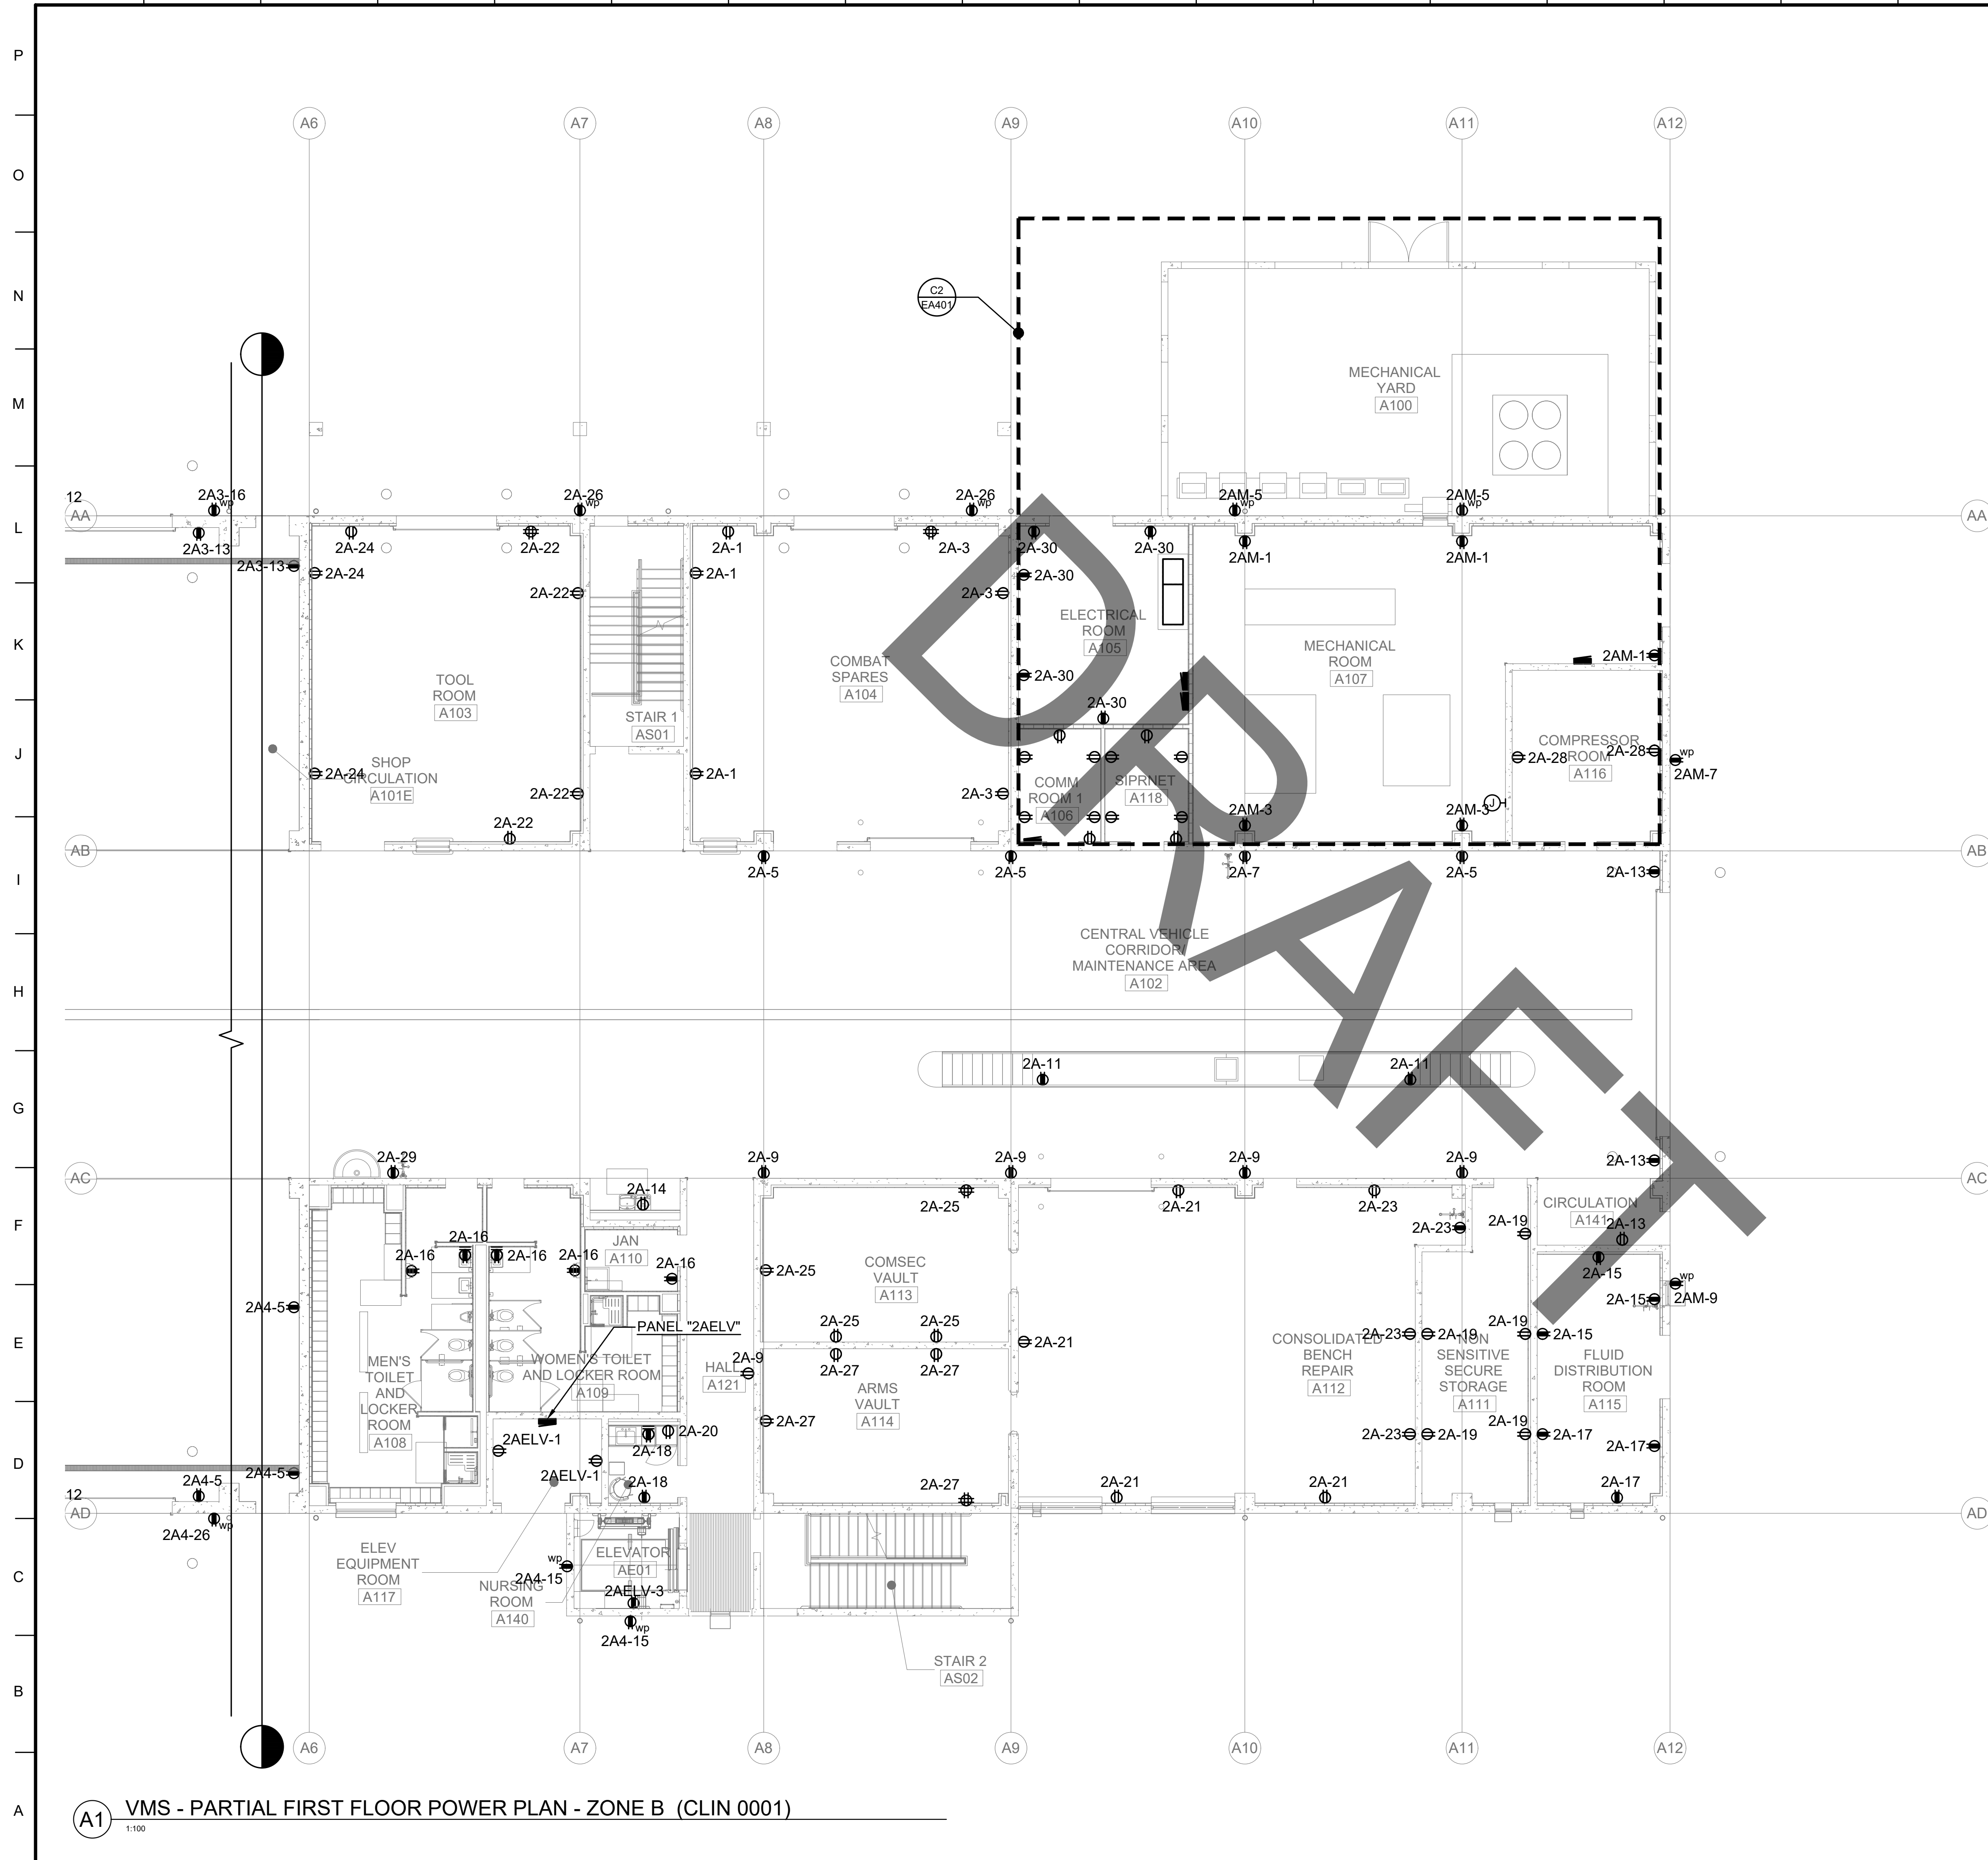


— P
— O
— N
— M
— L
— K
— J
— I
— H
— G
— F
— E
— D
— C
— B
— A

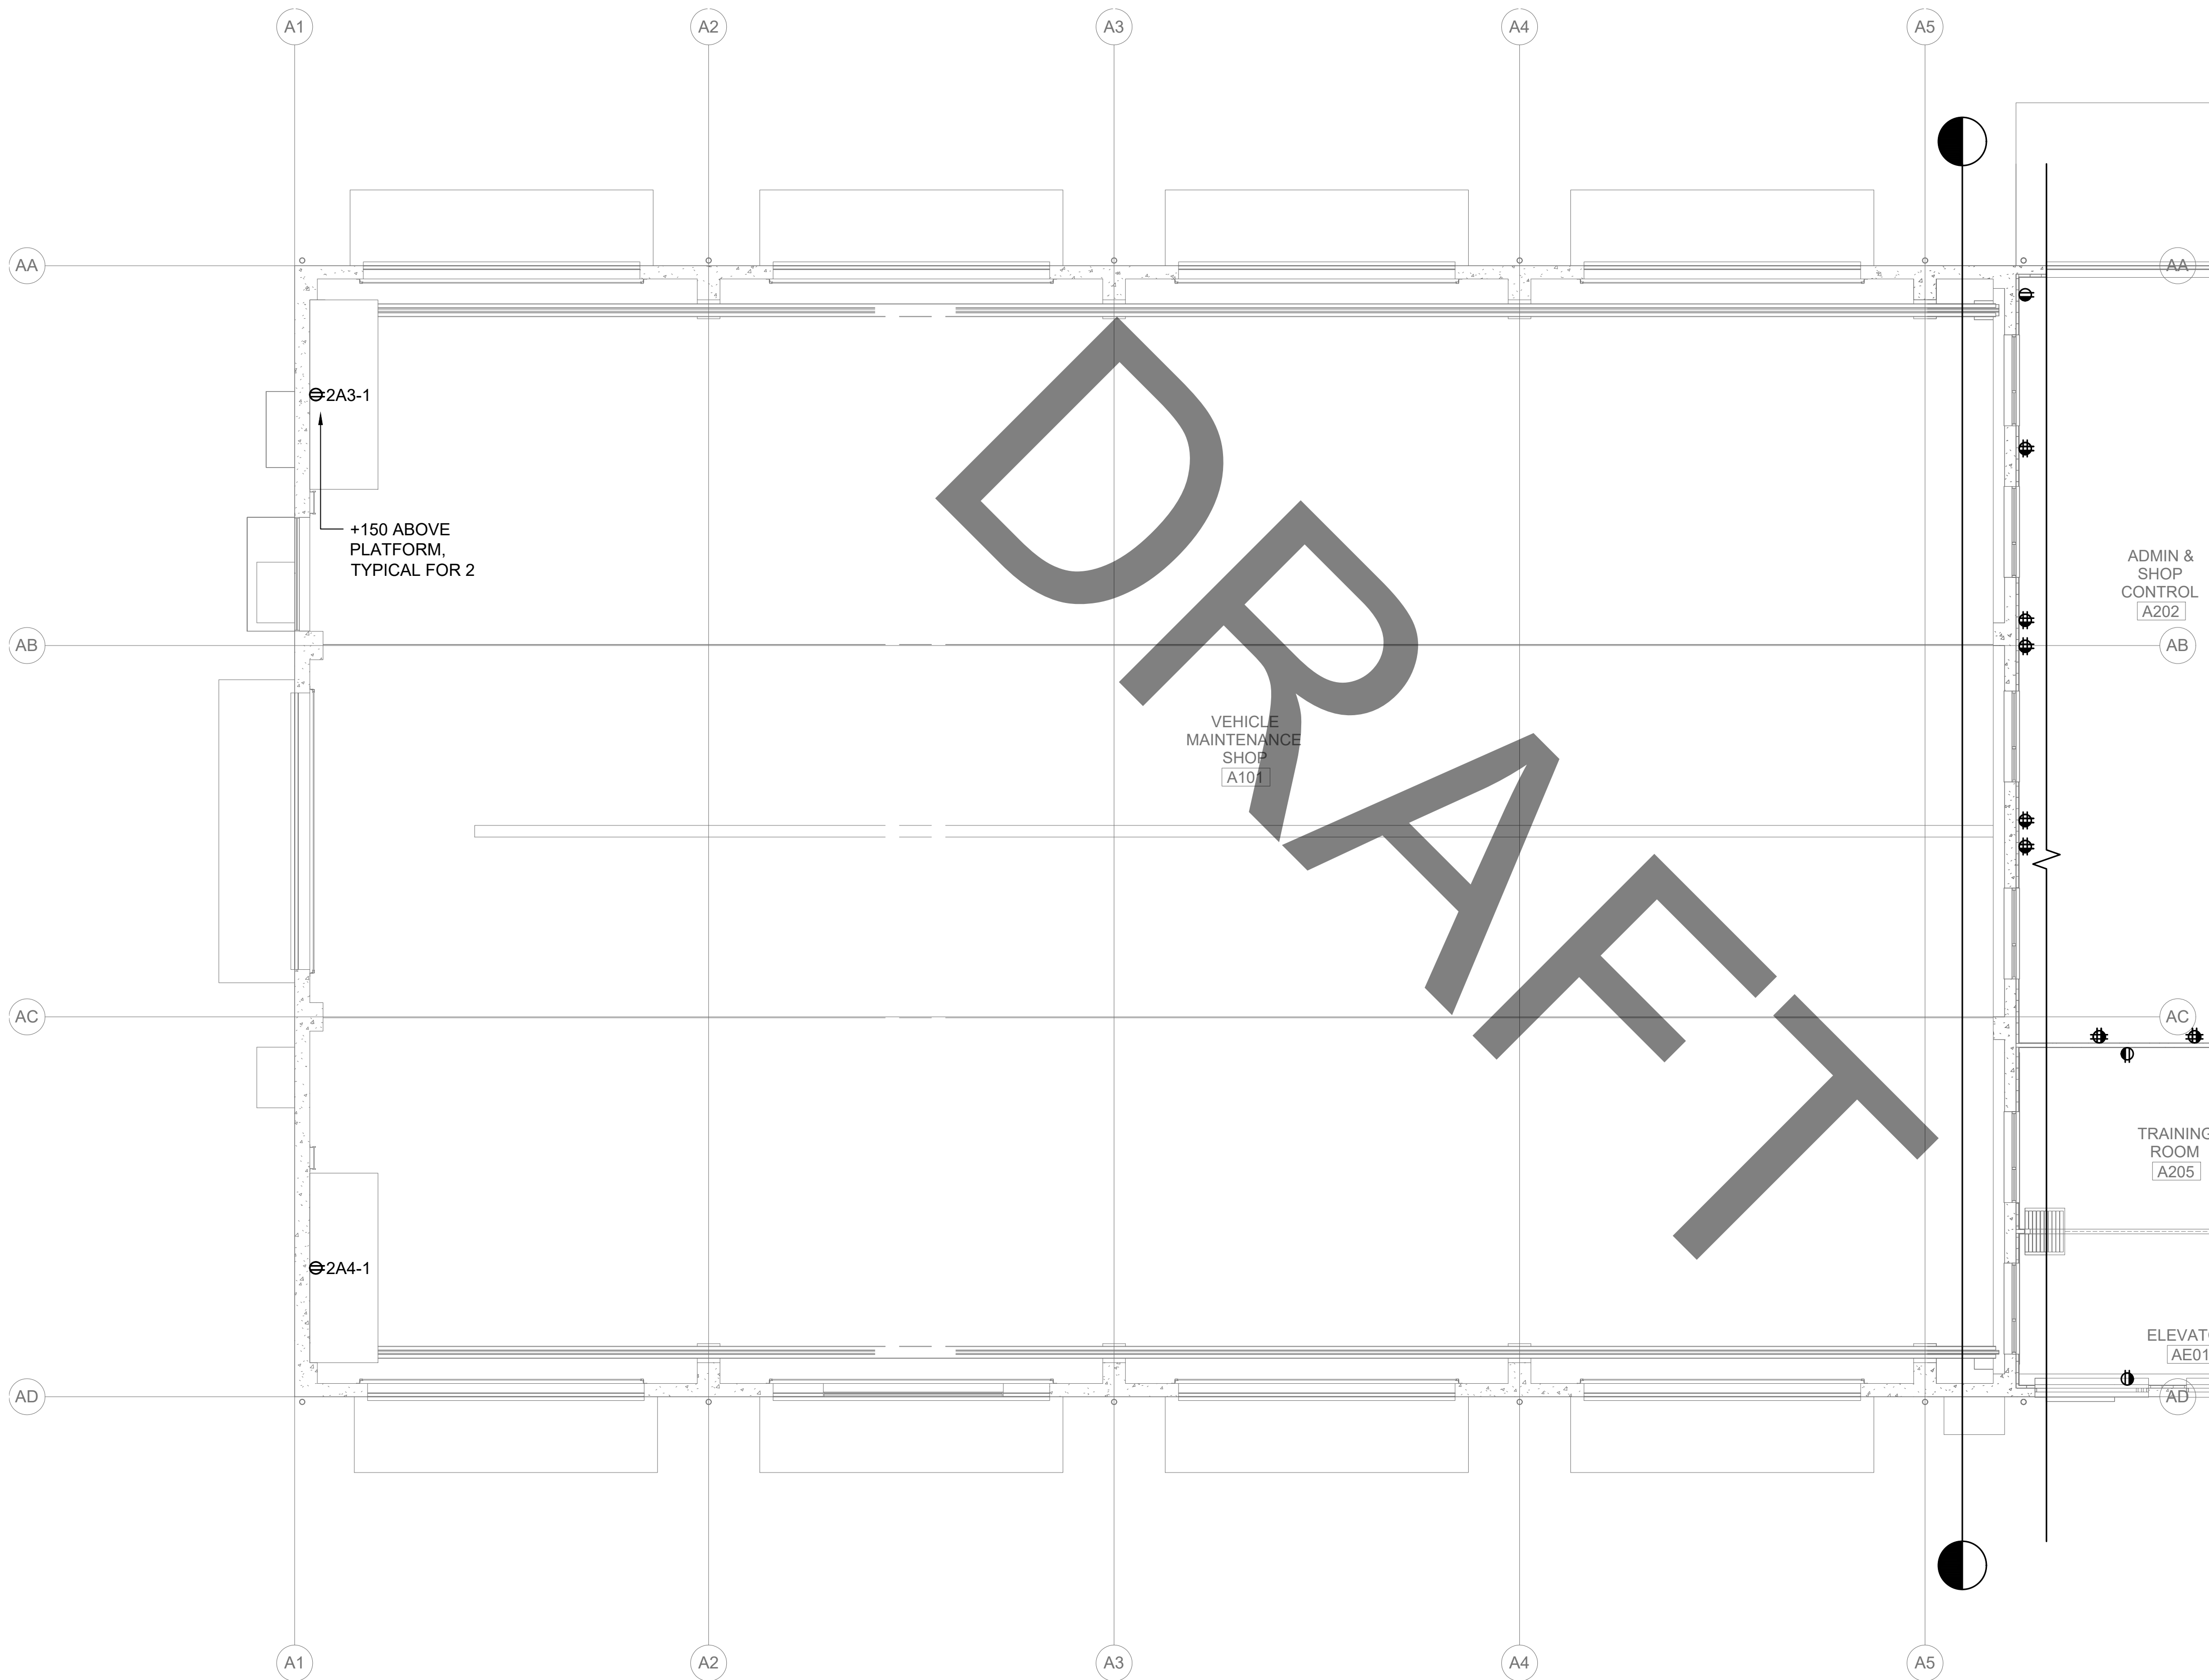

A1 VMS - PARTIAL SECOND FLOOR POWER PLAN - ZONE A (CLIN 0001)
1:100

GENERAL NOTES

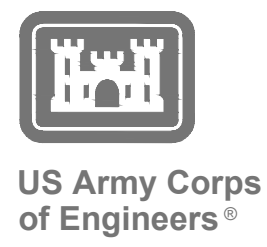[illegible]

US ARMY CORPS OF ENGINEERS JAPAN DISTRICT, OKINAWA AREA OFFICE USAED-J, UNIT 35132 APO, AP 96374-5132  SSPM INTERNATIONAL, INC. 500 KALANIANA'OLANI BLVD, #20 HONOLULU, HAWAII 96817	DESIGNED BY:	ISSUE DATE:
	DRAWN BY:	SOLICITATION NO.:
	CHECKED BY:	CONTRACT NO.:
	SUBMITTED BY:	SCALE: AS SHOWN
	SIZE: ISO A1	FILE NAME:

KADEIMA AIR BASE, OKINAWA, JAPAN
VEHICLE MAINTENANCE SHOP
FY20 MCA PN77833

SHEET ID


EA113

LEGEND

CLIN 0001

KEY PLAN


VMS - LEVEL 2
N.T.S.

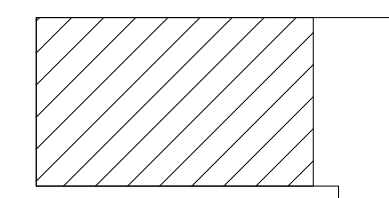


GRAPHIC SCALE




SCALE: 1 : 100

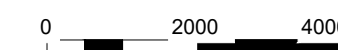

ALL DIMENSIONS AND/OR DIMENSIONS SHOWN IN
CALLOUT/ NOTES ARE IN MILLIMETERS UNLESS
OTHERWISE NOTED.

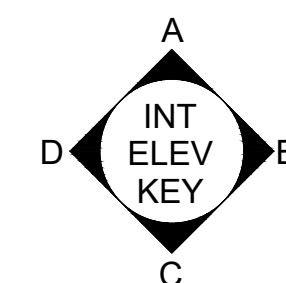


INTERMEDIATE DESIGN

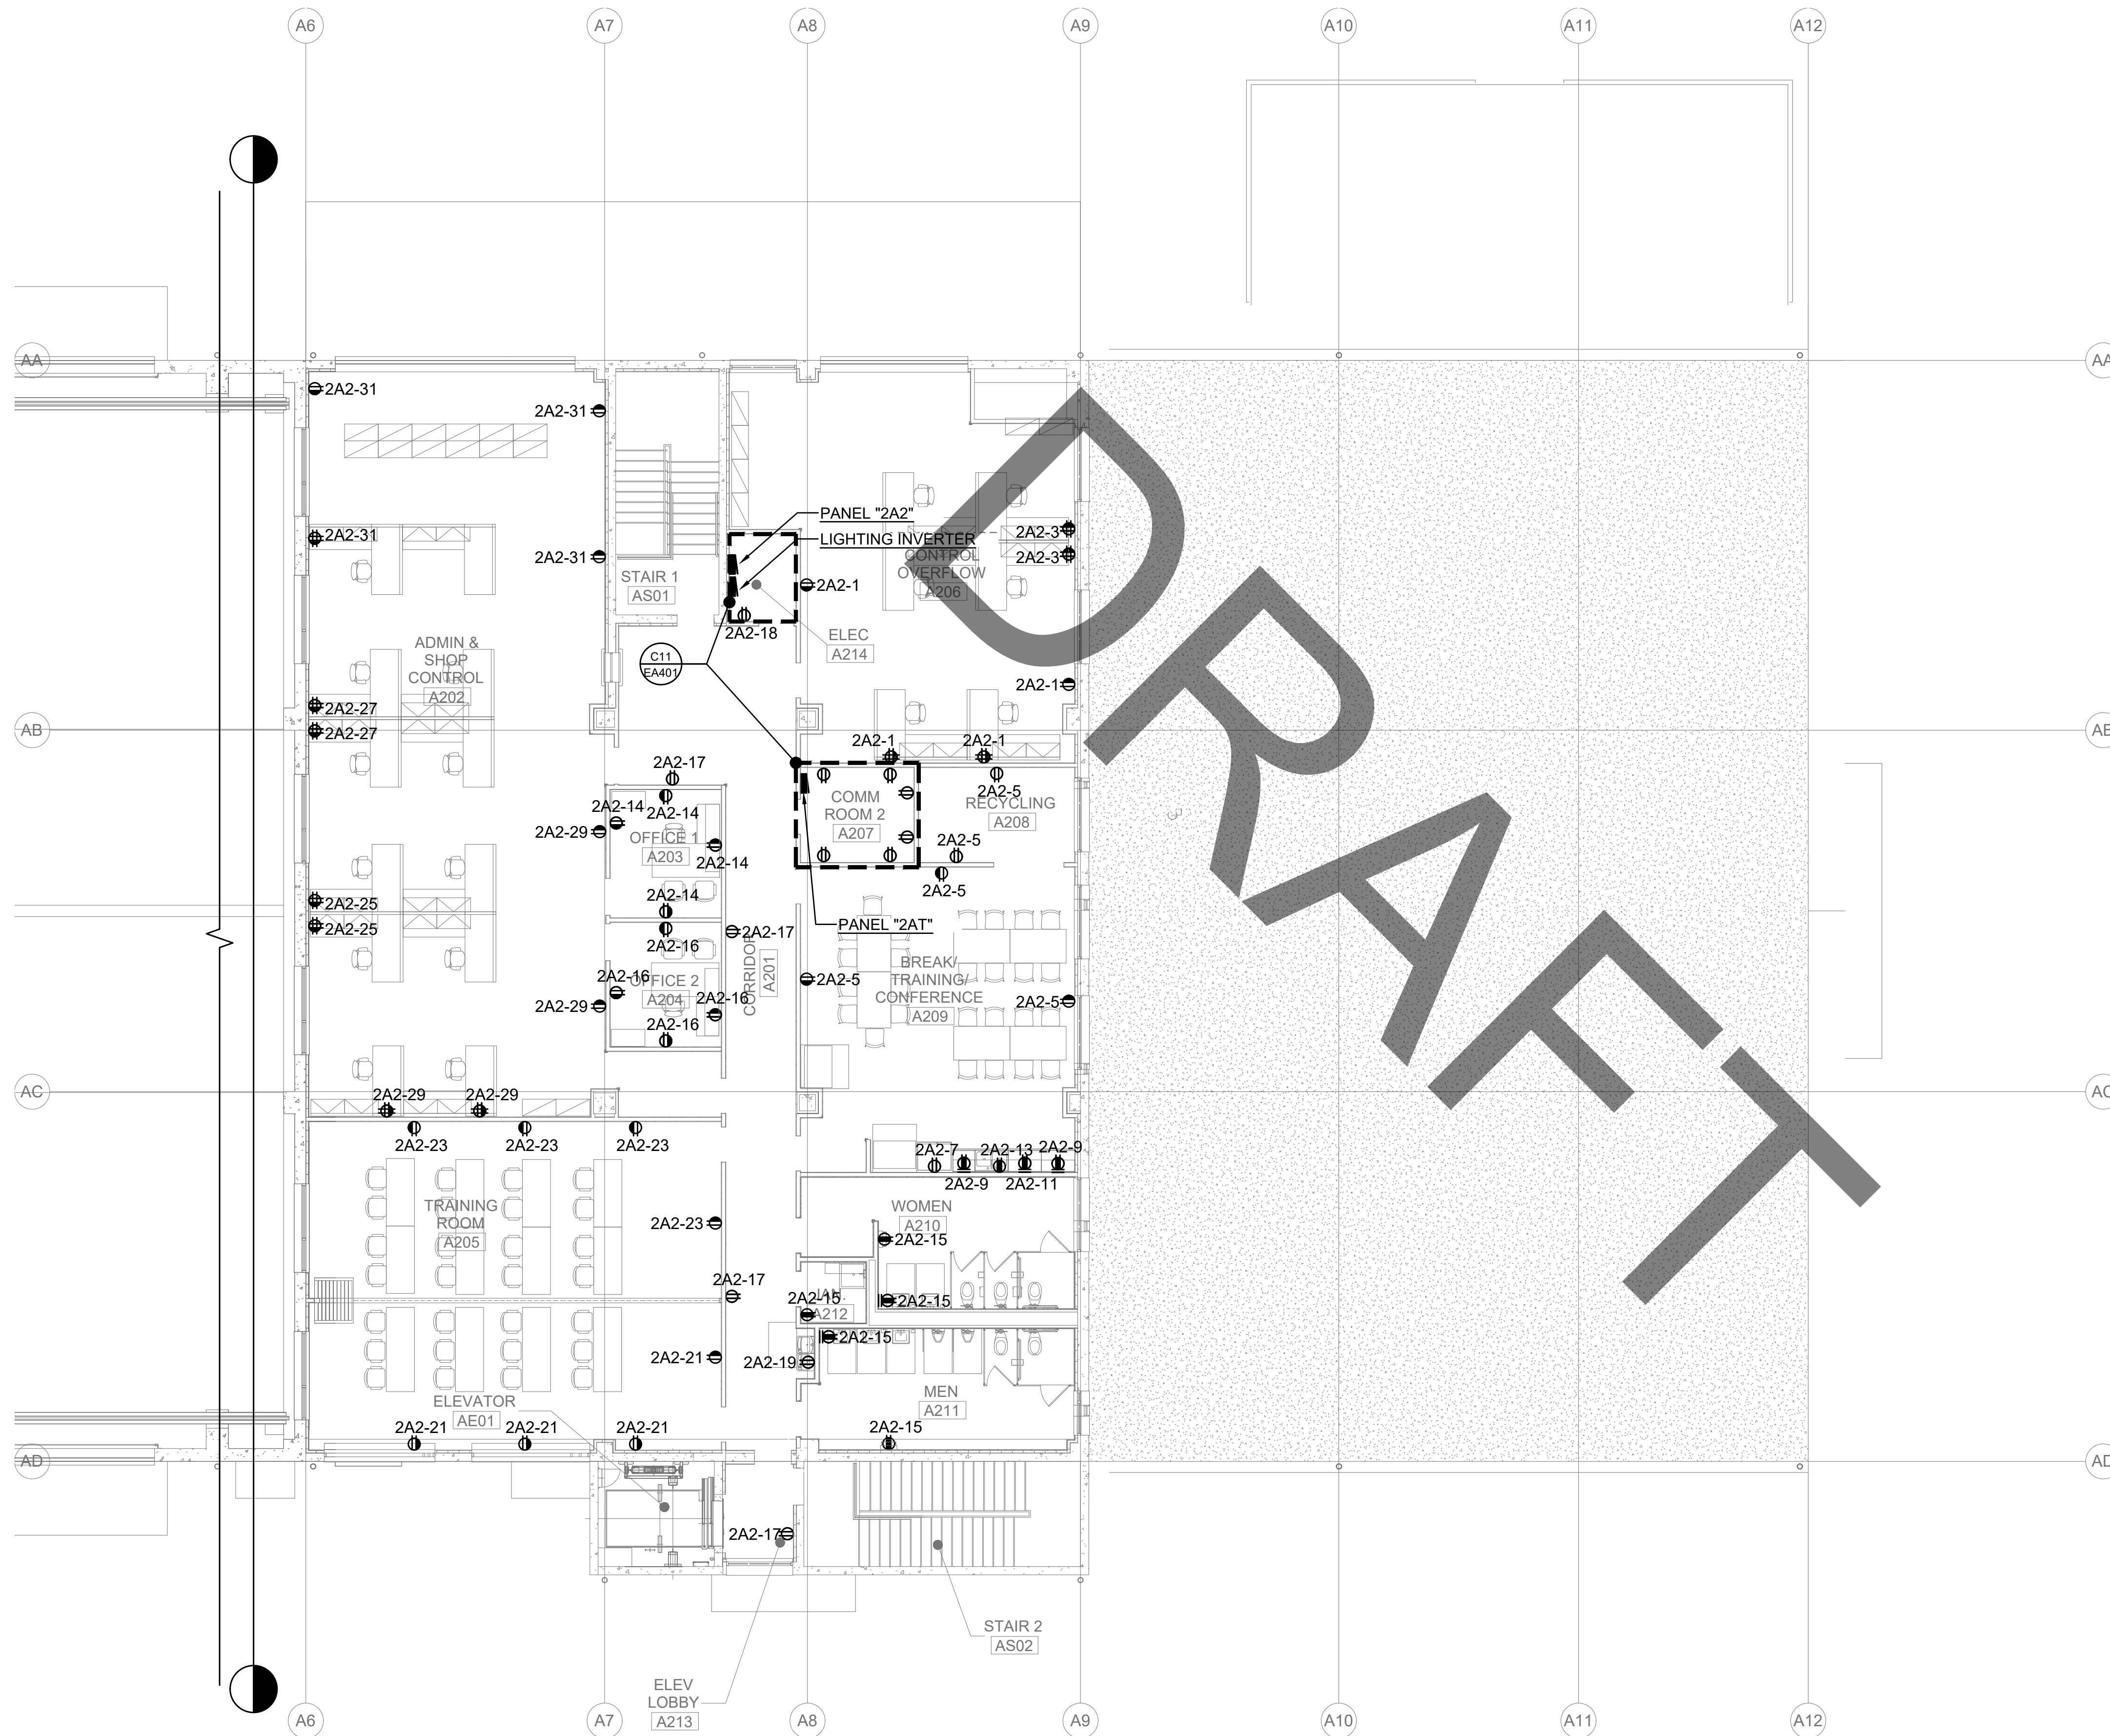

A1 VMS - PARTIAL SECOND FLOOR POWER PLAN - ZONE B (CLIN 0001)
1:100

GENERAL NOTES

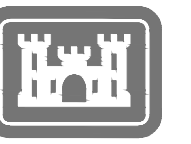

US Army Corps
of Engineers®


[illegible]

LEGEND

CLIN 0001

KEY PLAN


VMS - LEVEL 2
N.T.S.

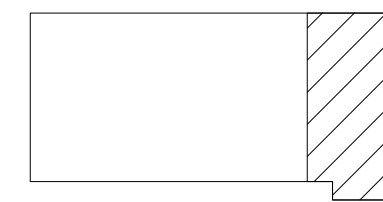

GRAPHIC SCALE



SCALE: 1 : 100

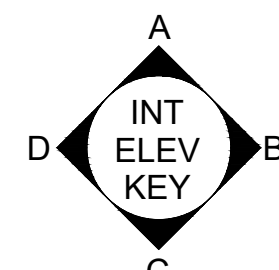

ALL DIMENSIONS AND/OR DIMENSIONS SHOWN IN
CALLOUT/ NOTES ARE IN MILLIMETERS UNLESS
OTHERWISE NOTED.

US ARMY CORPS OF ENGINEERS
JAPAN DISTRICT, OKINAWA AREA OFFICE
USAED-J, UNIT 35132

5555
PO, AP 96374-5132

**International
M INTERNATIONAL, INC**

501 SUMNER STREET, SUITE 620
HONOLULU, HAWAII 96817


KADENA AIR BASE, OKINAWA, JAPAN
VEHICLE MAINTENANCE SHOP
FY20 MCA PN77833

WMS - PARTIAL SECOND FLOOR POWER PLAN - ZONE B (CLIN 0001)

SHEET ID

E A 114

INTERMEDIATE DESIGN

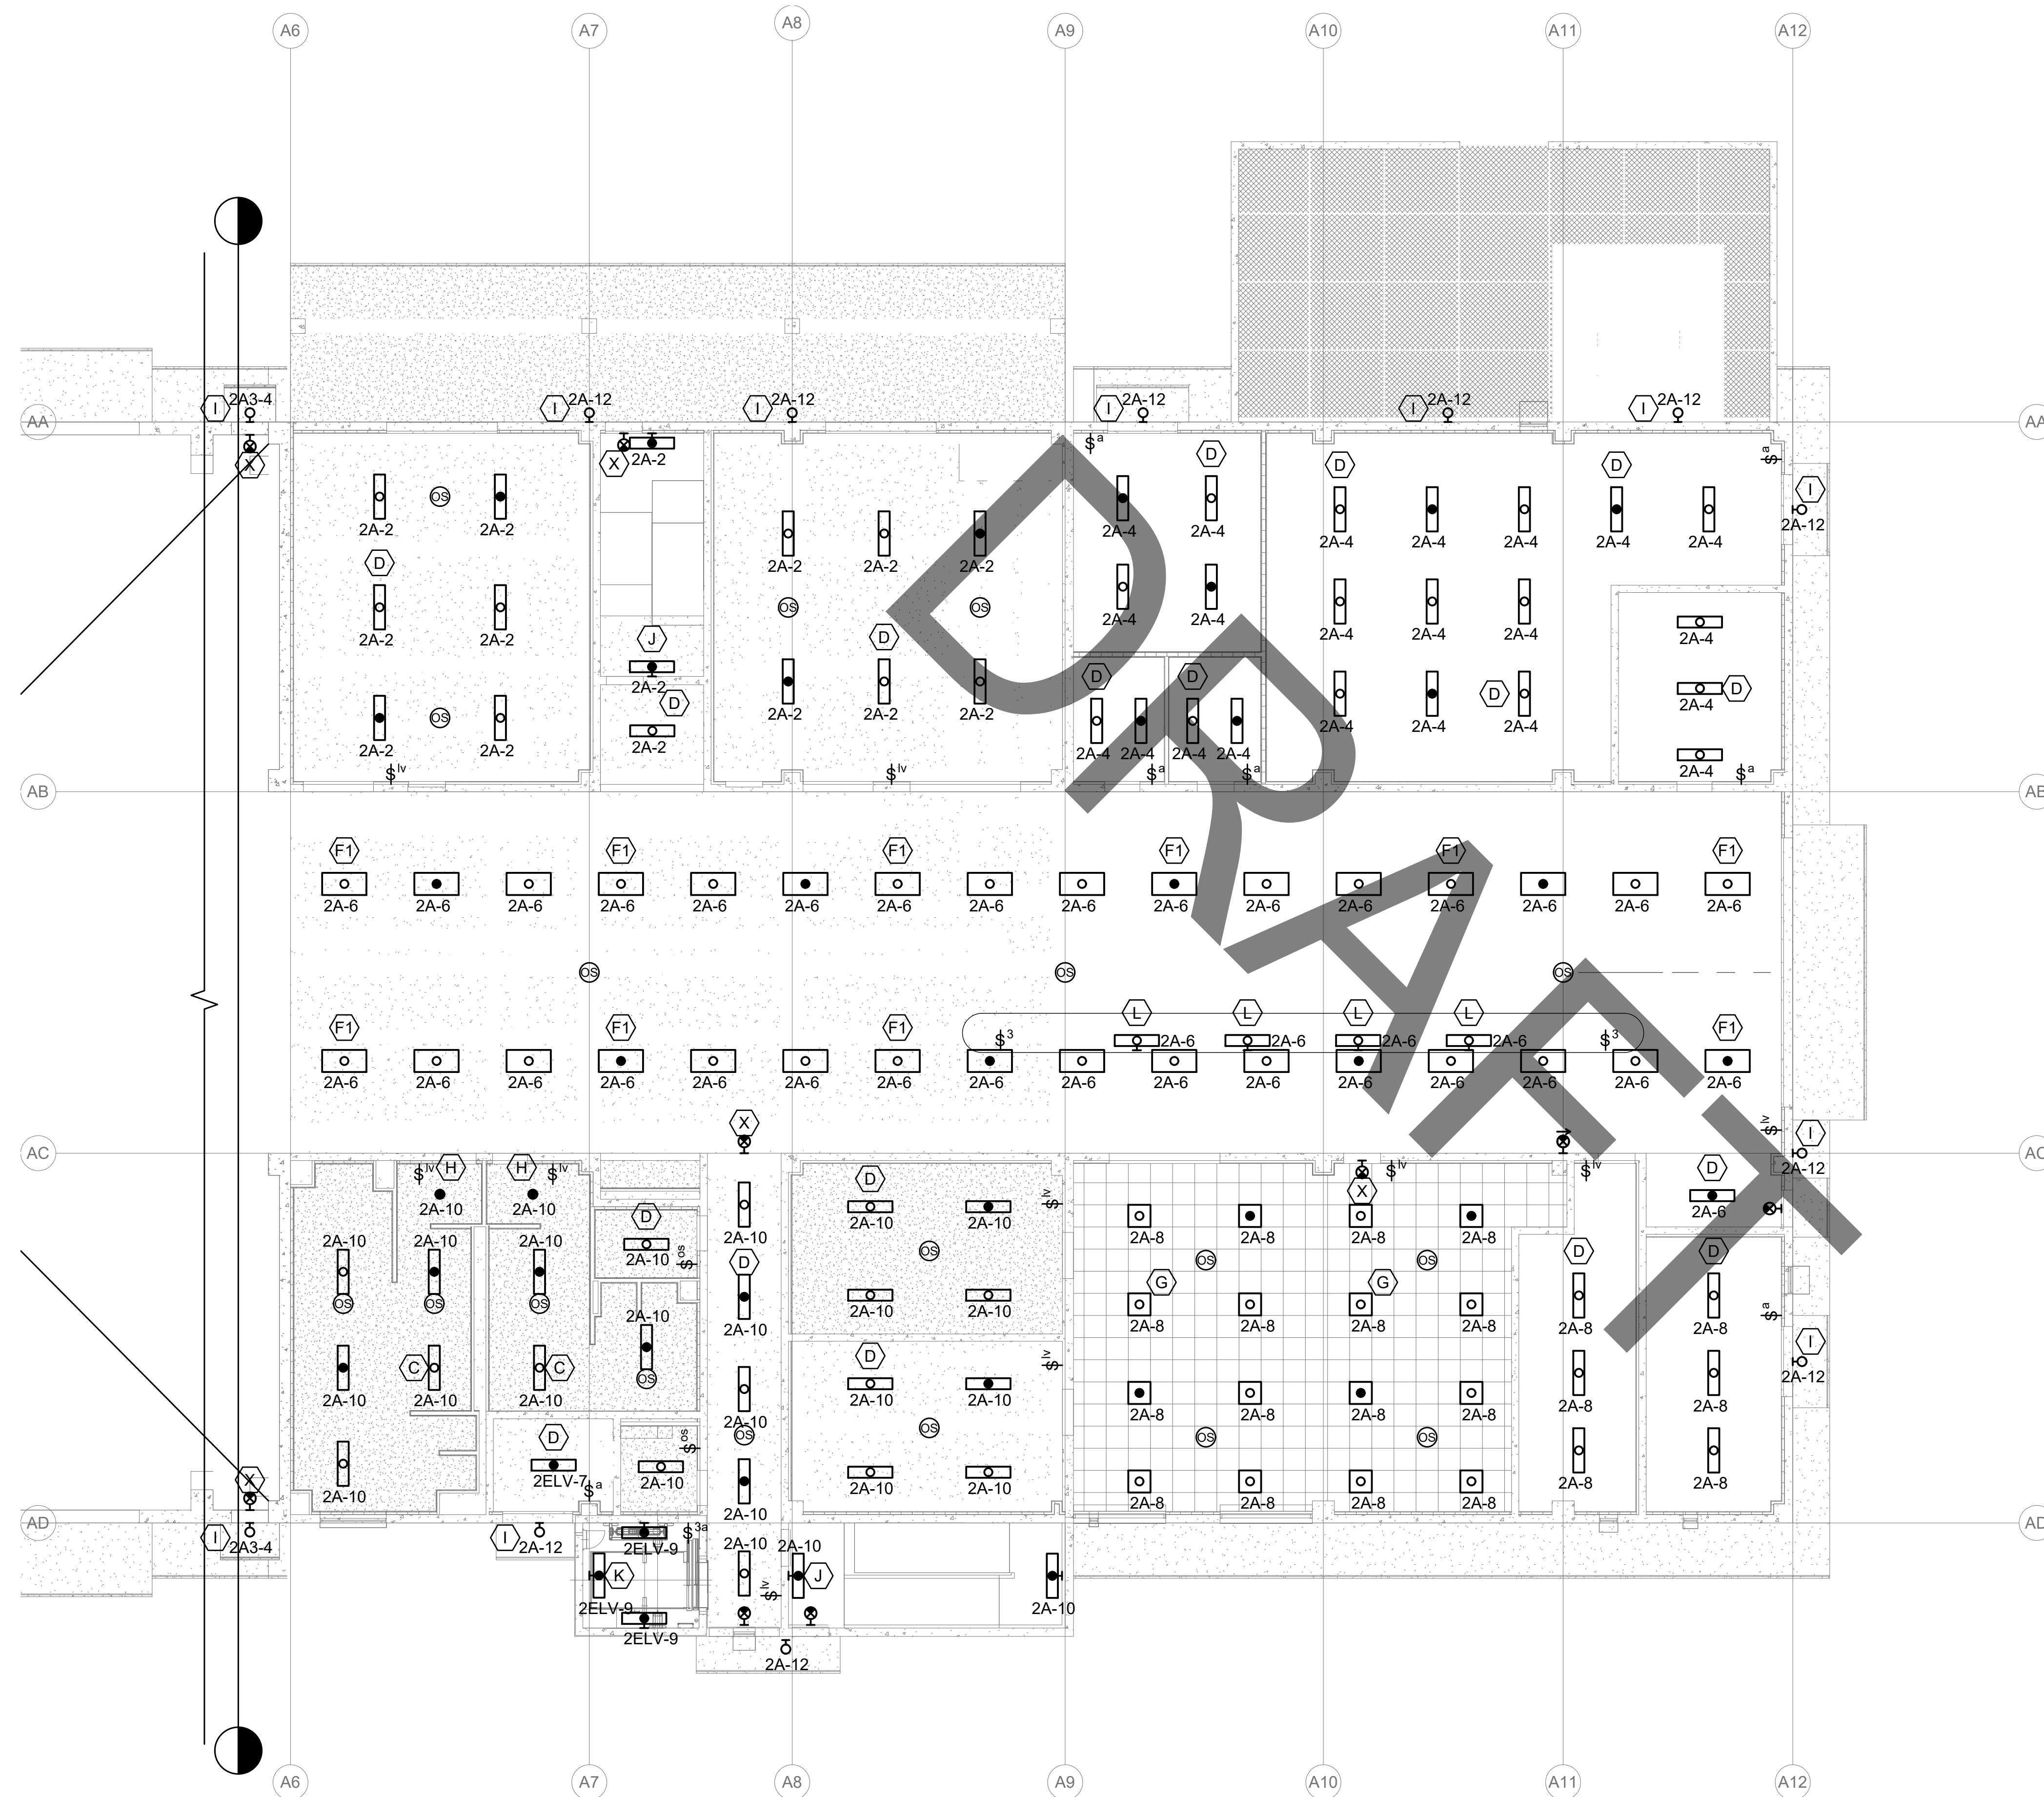


A1 VMS - PARTIAL FIRST FLOOR LIGHTING PLAN - ZONE B (CLIN 0001)
1:100

GENERAL NOTES

US Army Corps
of Engineers®

Item	Quantity	Unit	Price	Total
1. 1000	1000	kg	1000	1000
2. 1000	1000	kg	1000	1000
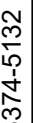US ARMY CORPS OF ENGINEERS JAPAN DISTRICT, OKINAWA AREA OFFICE USAED-J, UNIT 35132 APO, AP 96374-1132		DESIGNED BY: DRAWN BY: CHECKED BY: SUBMITTED BY: SIZE:	ISSUE DATE: SOLICITATION NO.: CONTRACT NO.: SCALE: FILE NAME:
 SPS INTERNATIONAL, INC. 501 SUMNER STREET, SUITE 620			

KADENA AIR BASE, OKINAWA, JAPAN
VEHICLE MAINTENANCE SHOP
FY20 MCA PN7833

VMS - PARTIAL FIRST FLOOR LIGHTING PLAN - ZONE B (CLIN 0001)

SHEET ID


EA122

INTERMEDIATE DESIGN

CLIN 0001

KEY PLAN



VMS - LEVEL 1
N.T.S.

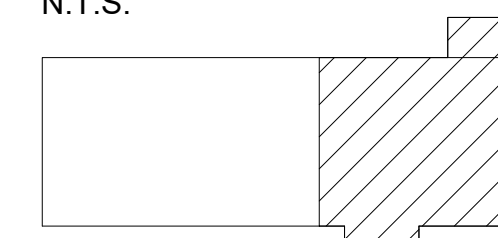

GRAPHIC SCALE



SCALE: 1 : 100

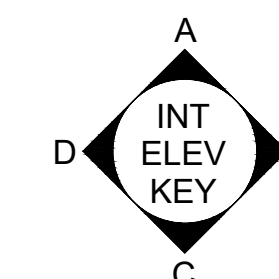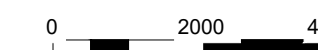

ALL DIMENSIONS AND/OR DIMENSIONS SHOWN IN
CALLOUT/ NOTES ARE IN MILLIMETERS UNLESS
OTHERWISE NOTED.

US Army Corps
of Engineers®

...	...
-----	-----

DESIGNED BY: _____ ISSUE DATE: _____

US ARMY CORPS OF ENGINEERS
JAPAN DISTRICT, OKINAWA AREA OFFICE

CONTRACT NO.:

CHECKED BY:

USAED-J, UNIT 35132
APO, AP 96374-5132

USAED-J, UNIT 35132
APO, AP 96374-5132

USAED-J, UNIT 35132
APO, AP 96374-5132

WMS - PARTIAL SECOND FLOOR LIGHTING PLAN - ZONE A (CLIN 0001)

SHEET ID

EA123


INTERMEDIATE DESIGN

KEY PLAN

VMS - LEVEL 2
N.T.S.

GRAPHIC SCALE

PLAN
NORTH

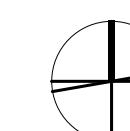

SCALE: 1 : 100

ALL DIMENSIONS AND/OR DIMENSIONS SHOWN IN
CALLOUT/ NOTES ARE IN MILLIMETERS UNLESS
OTHERWISE NOTED

VMS - PARTIAL SECOND FLOOR LIGHTING PLAN - ZONE A (CLIN 0001)

1:10

[illegible]

JAPAN DISTRICT, OKINAWA AREA OFFICE USASD-J UNIT 35132 APO, AP 96374-5132		 SSFM INTERNATIONAL, INC 501 SUMMER STREET, SUITE 620	SOLICITATION NO.: CONTRACT NO.: SCALE: AS SHOWN
DRAWN BY:	CHECKED BY:	SUBMITTED BY:	FILE NAME:

MAZENKAR BASE, OKINAWA, JAPAN
VEHICLE MAINTENANCE SHOP
FY20 MCA PN77833

SHEET ID

EA131

INTERMEDIATE DESIGN

CLIN 0001



KEY PLAN

VMS - LEVEL 1
N.T.S.

SCALE: 1 : 100


Age Group	Number of People
0-14	~1500
15-24	~1800
25-34	~2200
35-44	~1800
45-54	~1500
55-64	~1200
65-74	~800
75+	~500

ALL DIMENSIONS AND/OR DIMENSIONS SHOWN IN
CALLOUT/ NOTES ARE IN MILLIMETERS UNLESS
OTHERWISE NOTED.

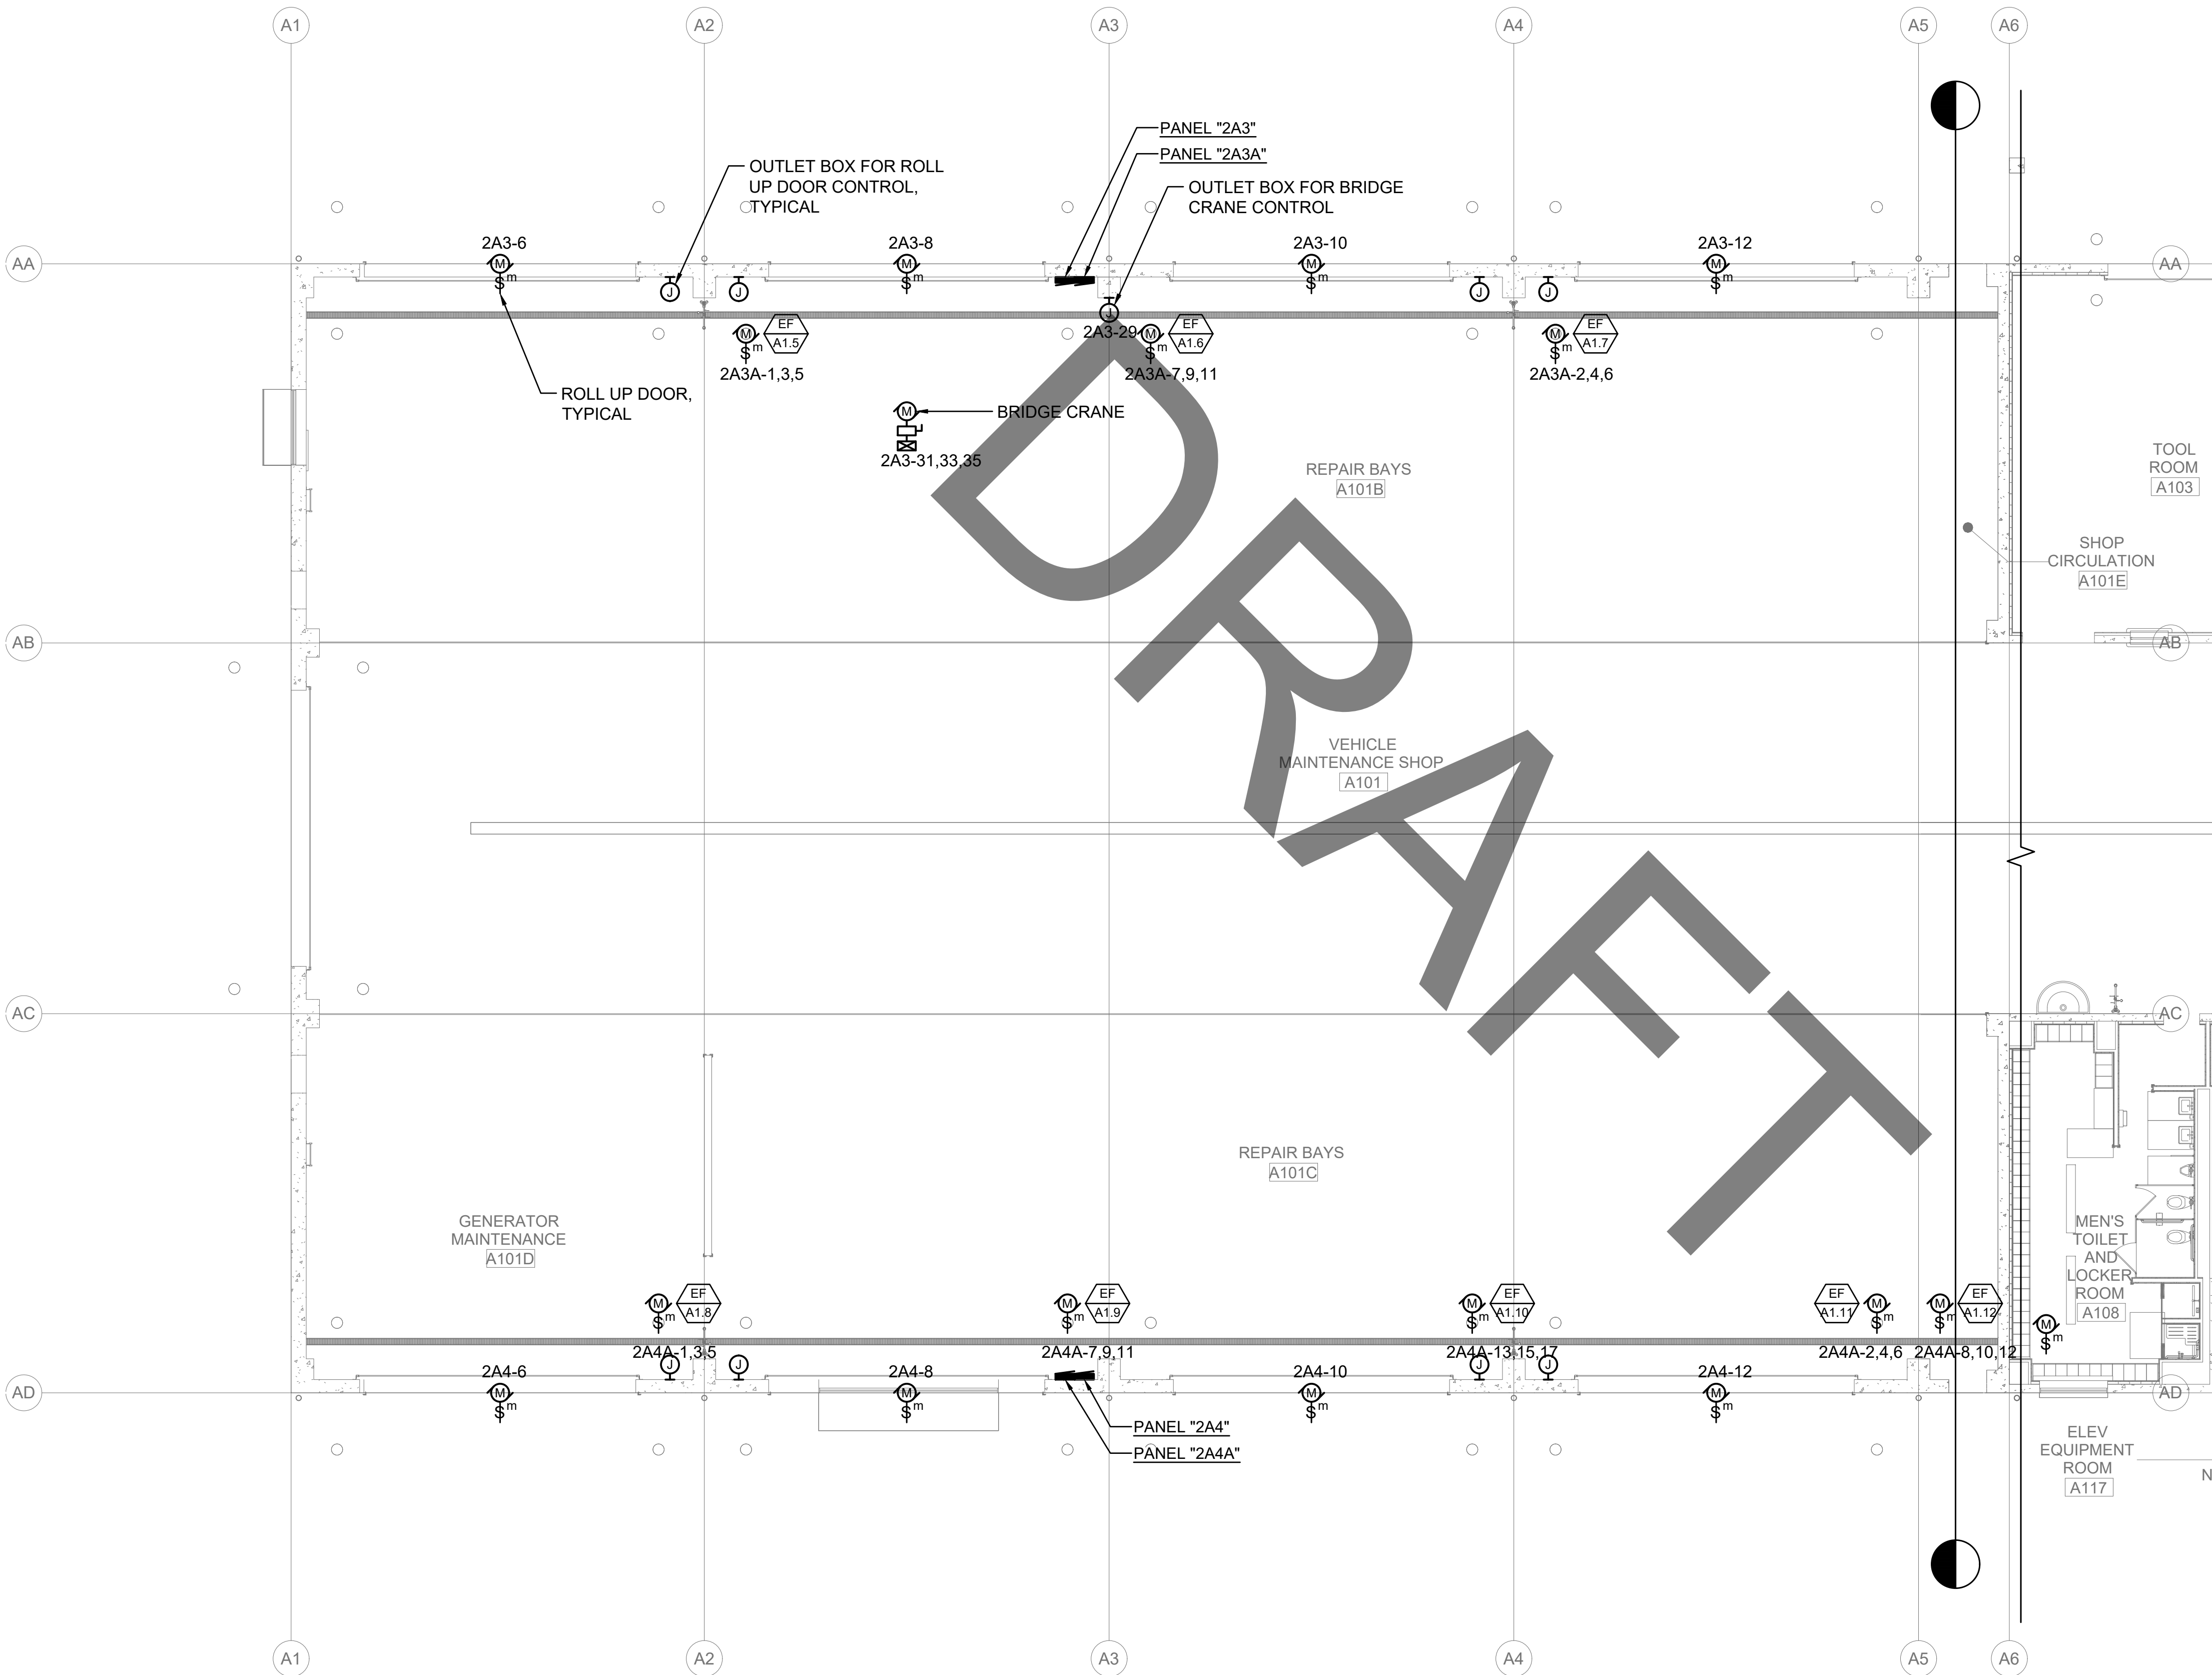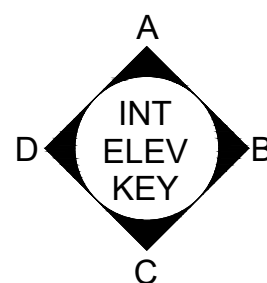

Λ1 VMS - PARTIAL FIRST FLOOR MECHANICAL EQUIPMENT POWER PLAN - ZONE A (CLIN 0001)

1:10

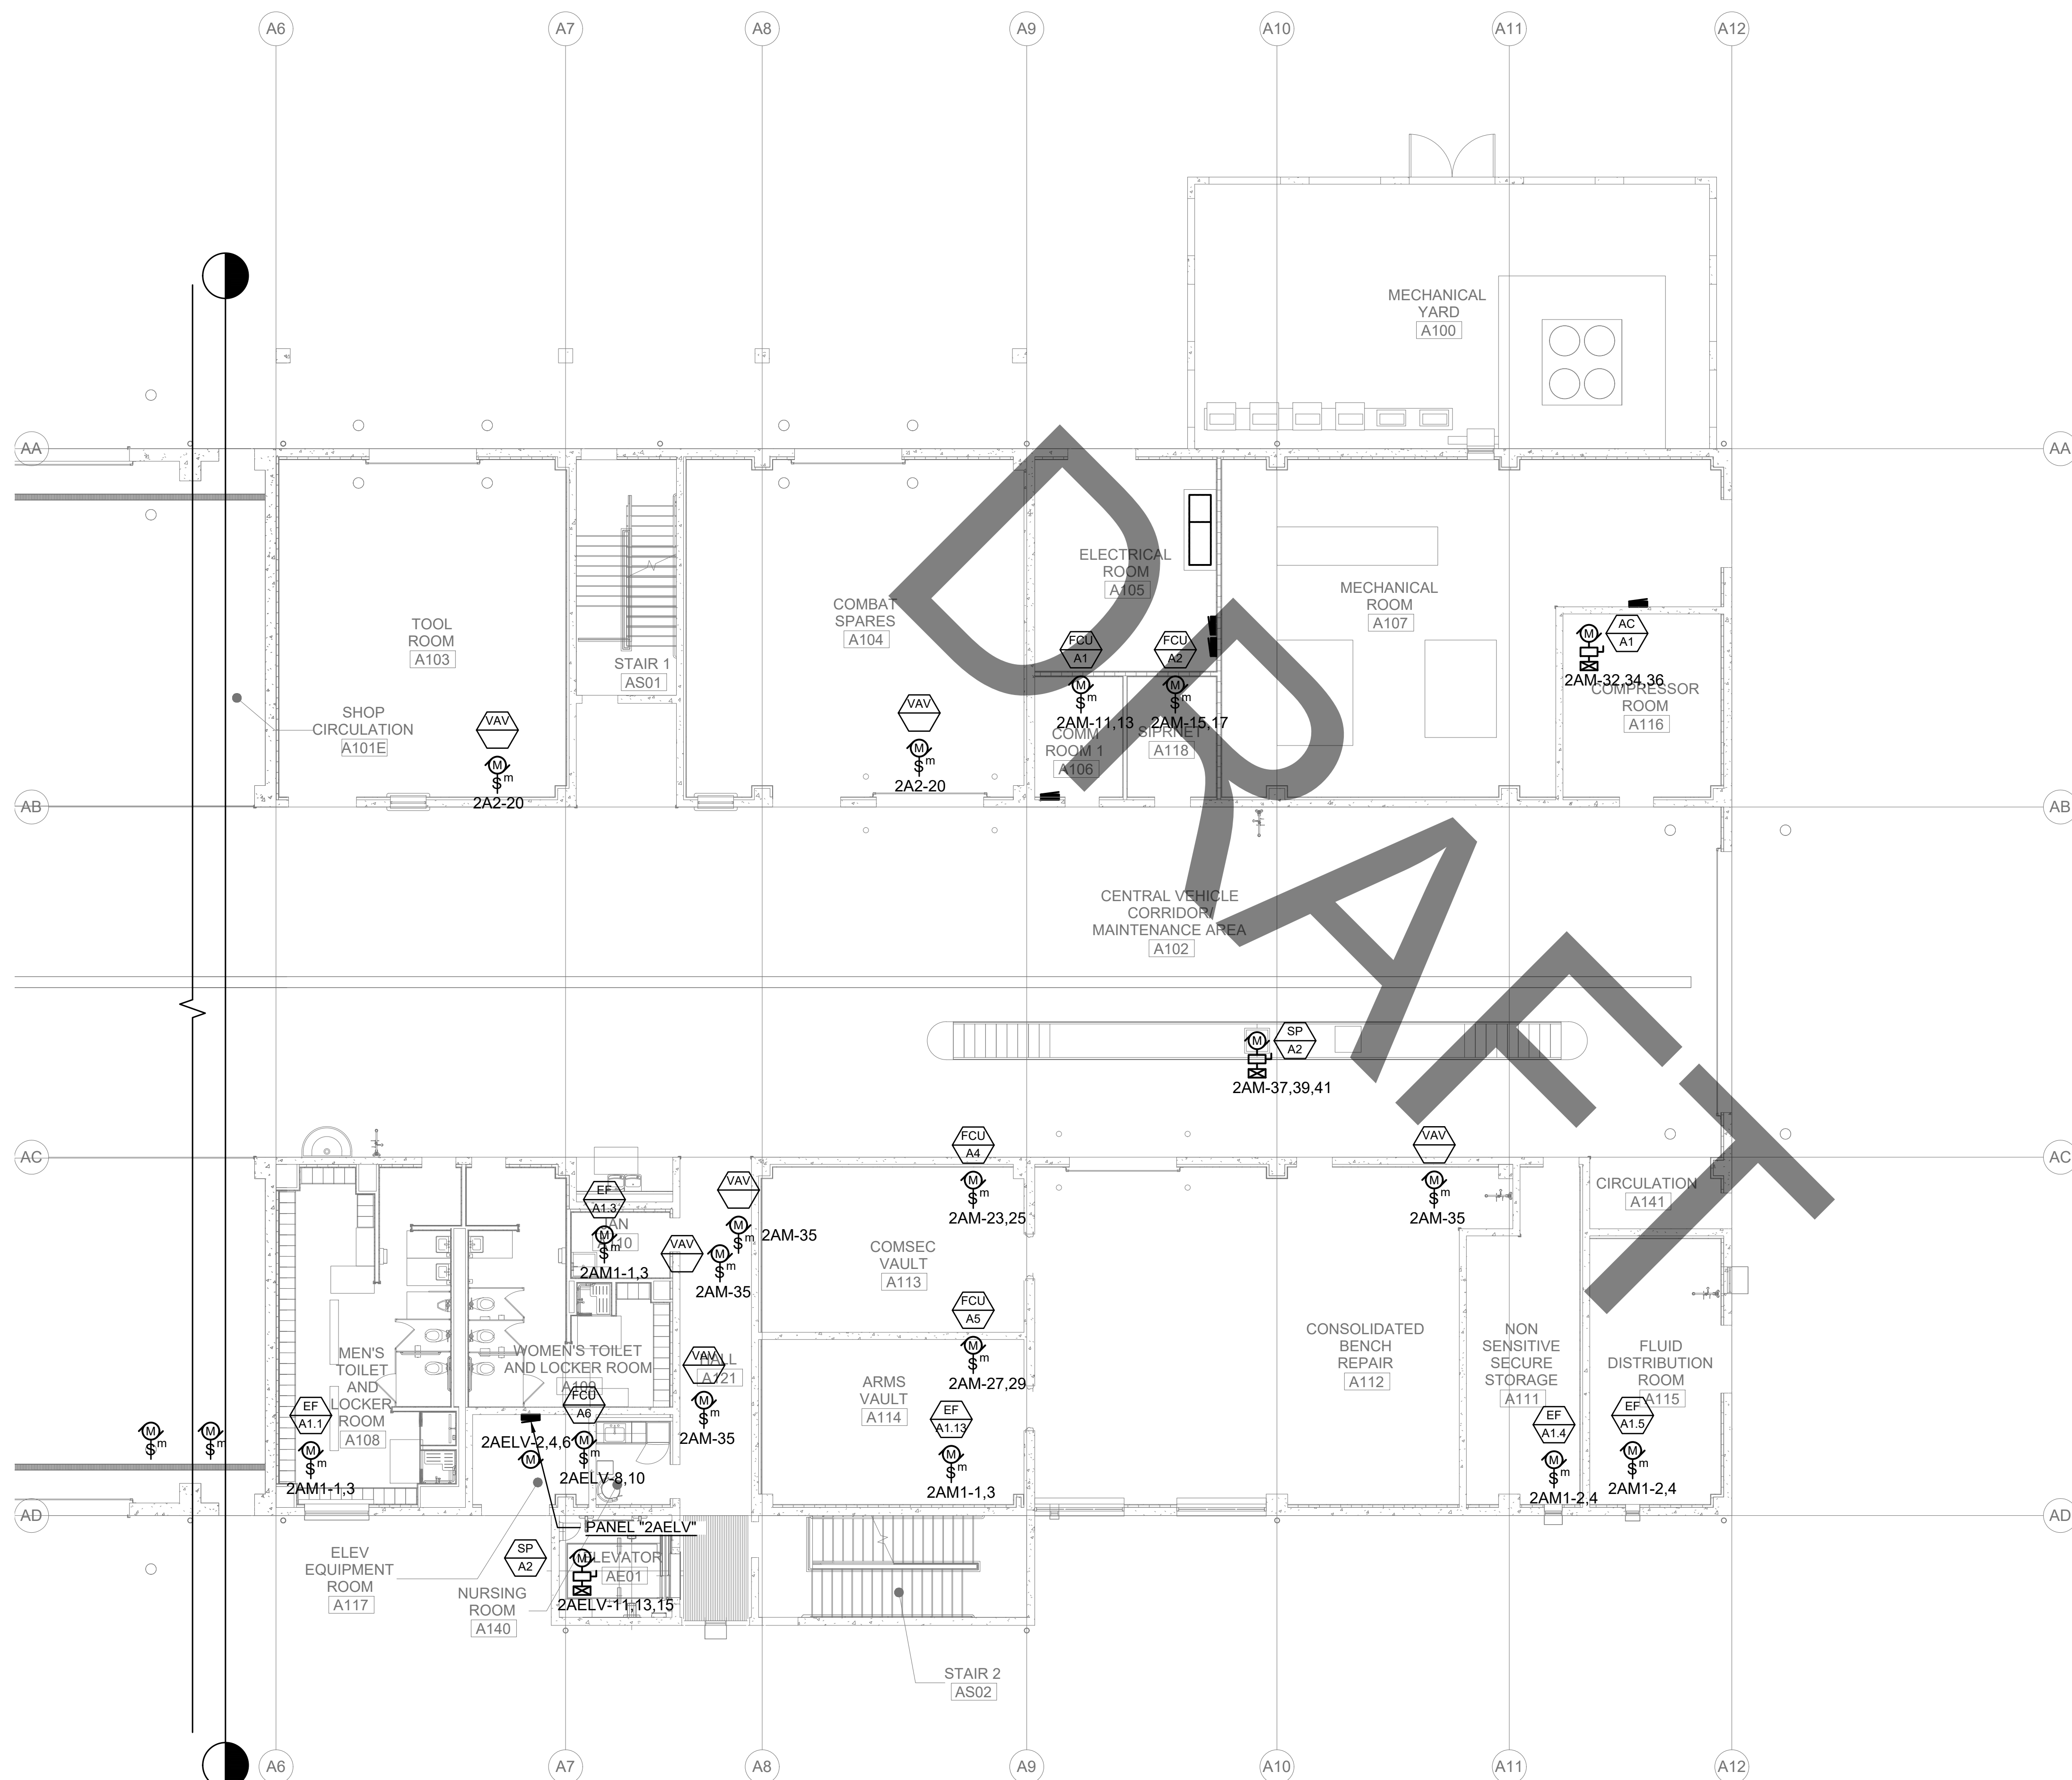

GENERAL NOTES



US Army Corps
of Engineers®

LEGEND

Item	Value	Unit
1. 1000	1000	1000
2. 1000	1000	1000
SSPM INTERNATIONAL SSPM INTERNATIONAL, INC 501 SUMNER STREET, SUITE 620	DESIGNED BY:	ISSUE DATE:
	DRAWN BY:	SOLICITATION NO.:
	CHECKED BY:	CONTRACT NO.:
	SUBMITTED BY:	SCALE:
	SIZE:	FILE NAME:

CLIN 0001


KEY PLAN

VMS - LEVEL 1


NTS

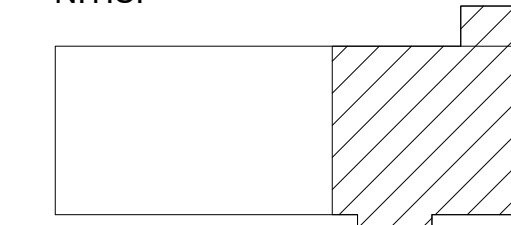

GRAPHIC SCALE

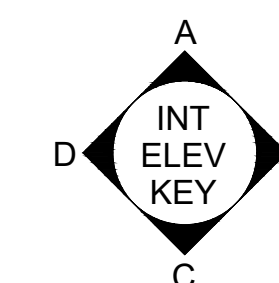

PLAN
NORTH

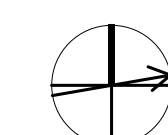

SCALE: 1 : 100

ALL DIMENSIONS AND/OR DIMENSIONS SHOWN IN
CALLOUT/ NOTES ARE IN MILLIMETERS UNLESS
OTHERWISE NOTED.

KADENA AIR BASE, OKINAWA, JAPAN
VEHICLE MAINTENANCE SHOP
FY20 MCA PN77833

SHEET ID

EA132

INTERMEDIATE DESIGN



US Army Corps
of Engineers®

[illegible]

US ARMY CORPS OF ENGINEERS JAPAN DISTRICT, OKINAWA AREA OFFICE USAED-J UNIT 35132 APO AF 96374-5132		DESIGNED BY: DRAWN BY: CHECKED BY: SUBMITTED BY: SCALE: AS SHOWN	ISSUE DATE: SOLICITATION NO.: CONTRACT NO.: FILE NAME: SIZE: A1
		SSPM INTERNATIONAL INC 501 SUMNER STREET, SUITE 620 HONOLULU, HAWAII 96817	

KADENA AIR BASE, OKINAWA, JAPAN
VEHICLE MAINTENANCE SHOP
FY20 MCA PN77833

SHEET ID

EA134



INTERMEDIATE DESIGN

KEY PLAN

VMS - LEVEL 2
N.T.S.



GRAPHIC SCALE

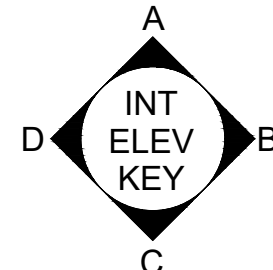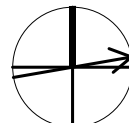
PLAN
NORTH

SCALE: 1 : 100

Age Group	Number of People
0	100
10	150
20	200
30	250
40	200
50	150
60	100
70	50
80	20
90	10
100	5

ALL DIMENSIONS AND/OR DIMENSIONS SHOWN IN
CALLOUT/ NOTES ARE IN MILLIMETERS UNLESS
OTHERWISE NOTED.


[illegible]

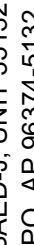US ARMY CORPS OF ENGINEERS JAPAN DISTRICT, OKINAWA AREA OFFICE USAEJ-1, UNIT 35132 APO, AP 96374-4132		DESIGNED BY: DRAWN BY: CHECKED BY: SUBMITTED BY:	ISSUE DATE: SOLICITATION NO.: CONTRACT NO.: SCALE: AS SHOWN
		S5F1 SUMMER STREET, SUITE 620 551 SUMMER STREET, SUITE 620	FILE NAME: SIZE:


KADENA AIR BASE, OKINAWA, JAPAN
VEHICLE MAINTENANCE SHOP
FY20 MCA PN77833

SHEET ID


EA401

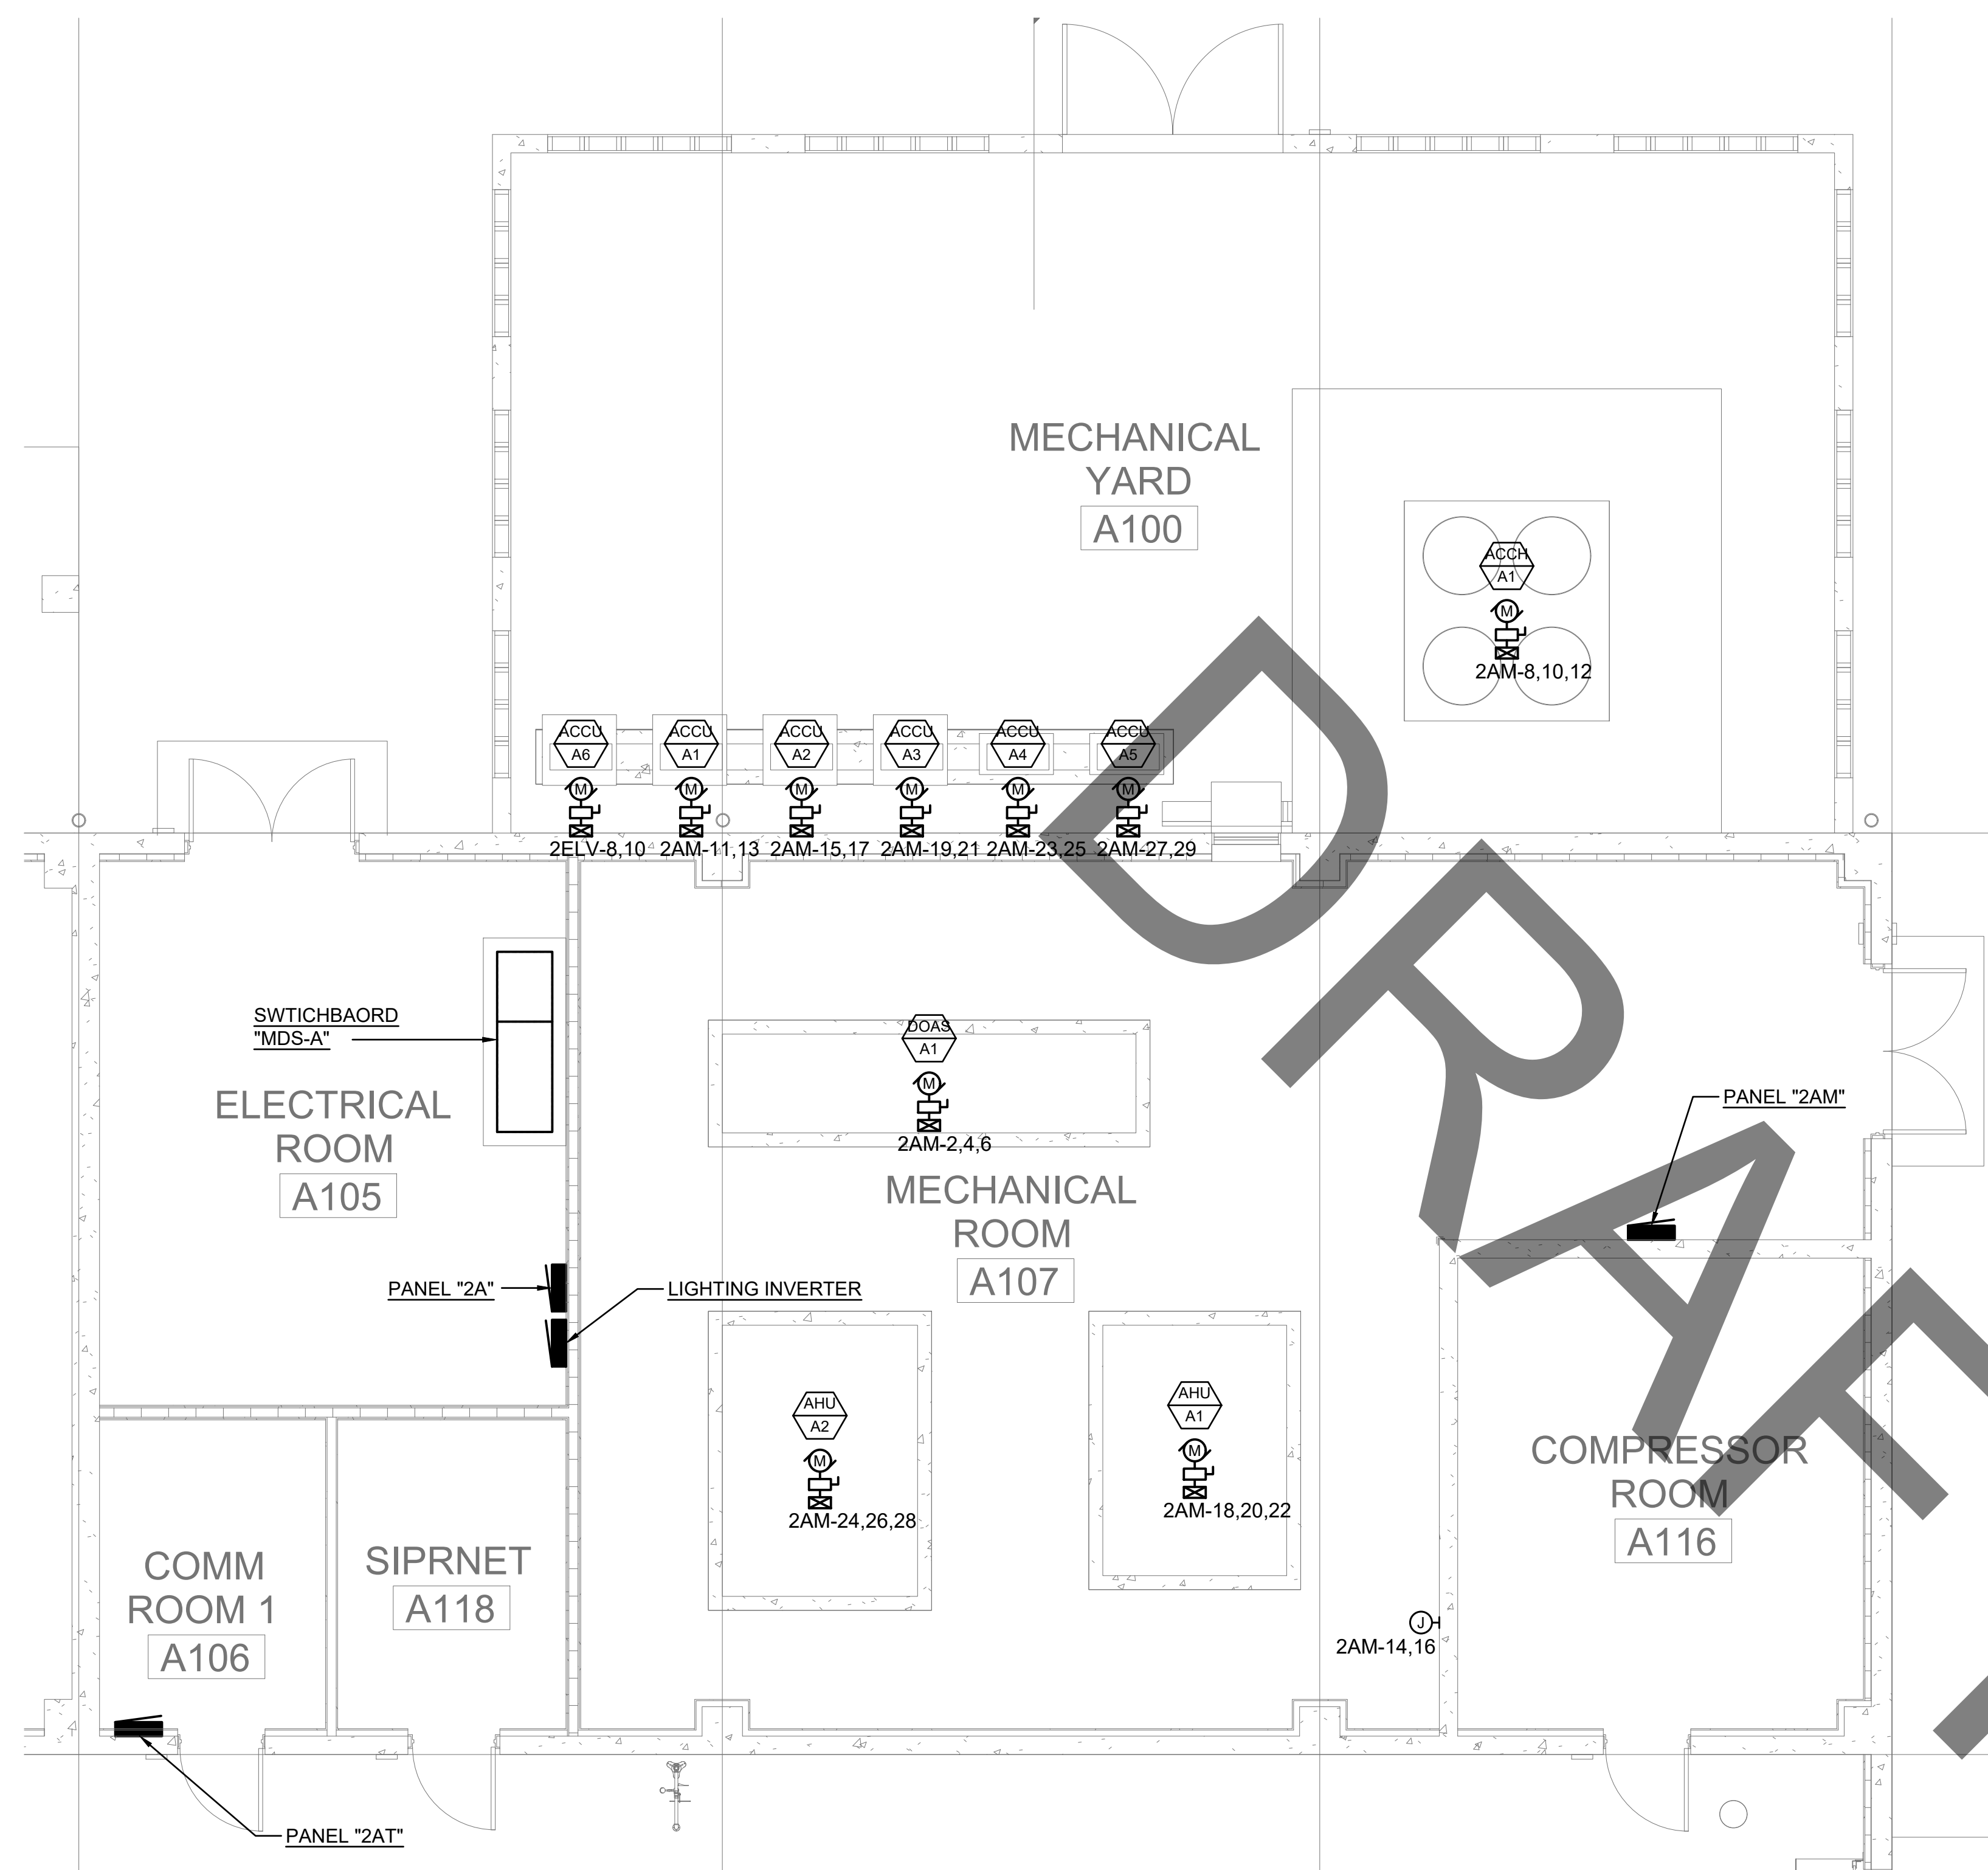


C2 1ST FLOOR ELEC, COMM, MECH ROOM
1:50

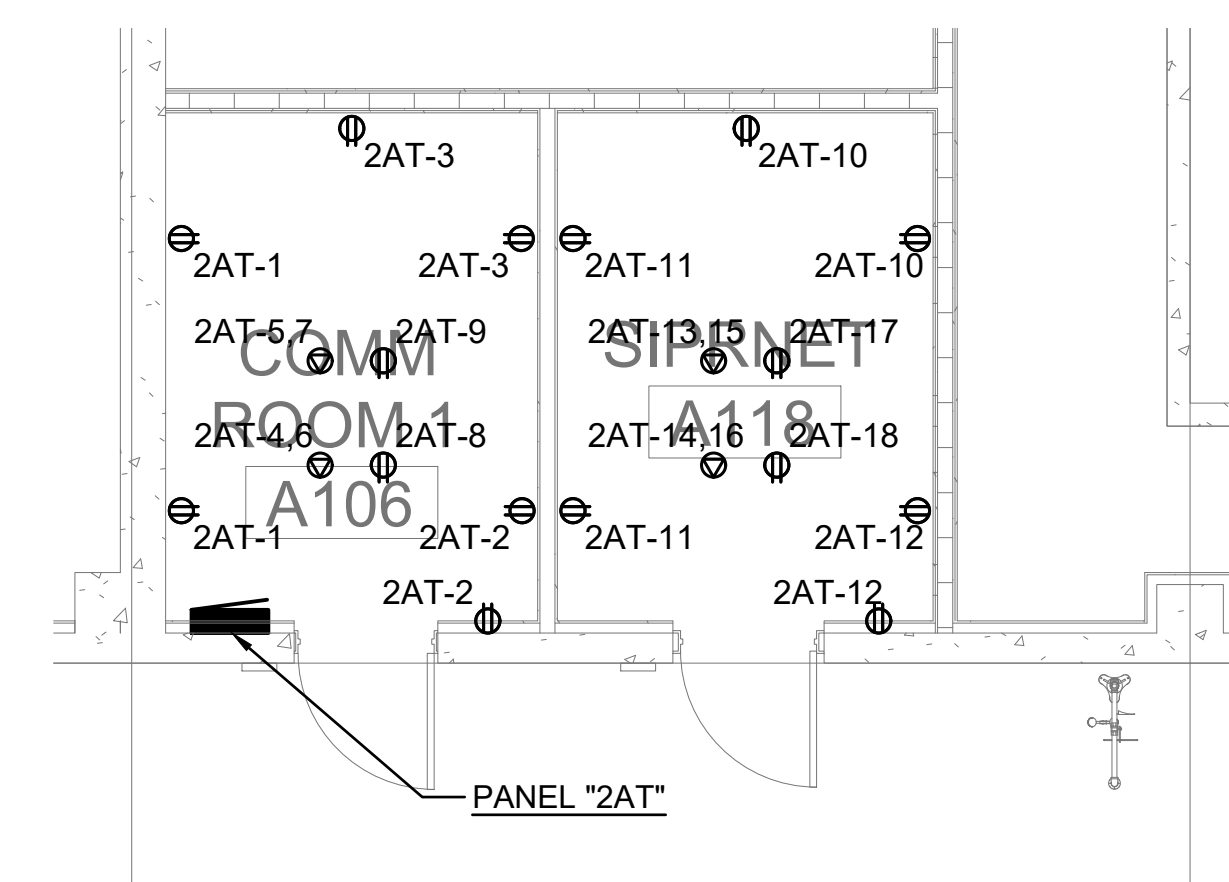

K11 1ST FLOOR COMM ROOM

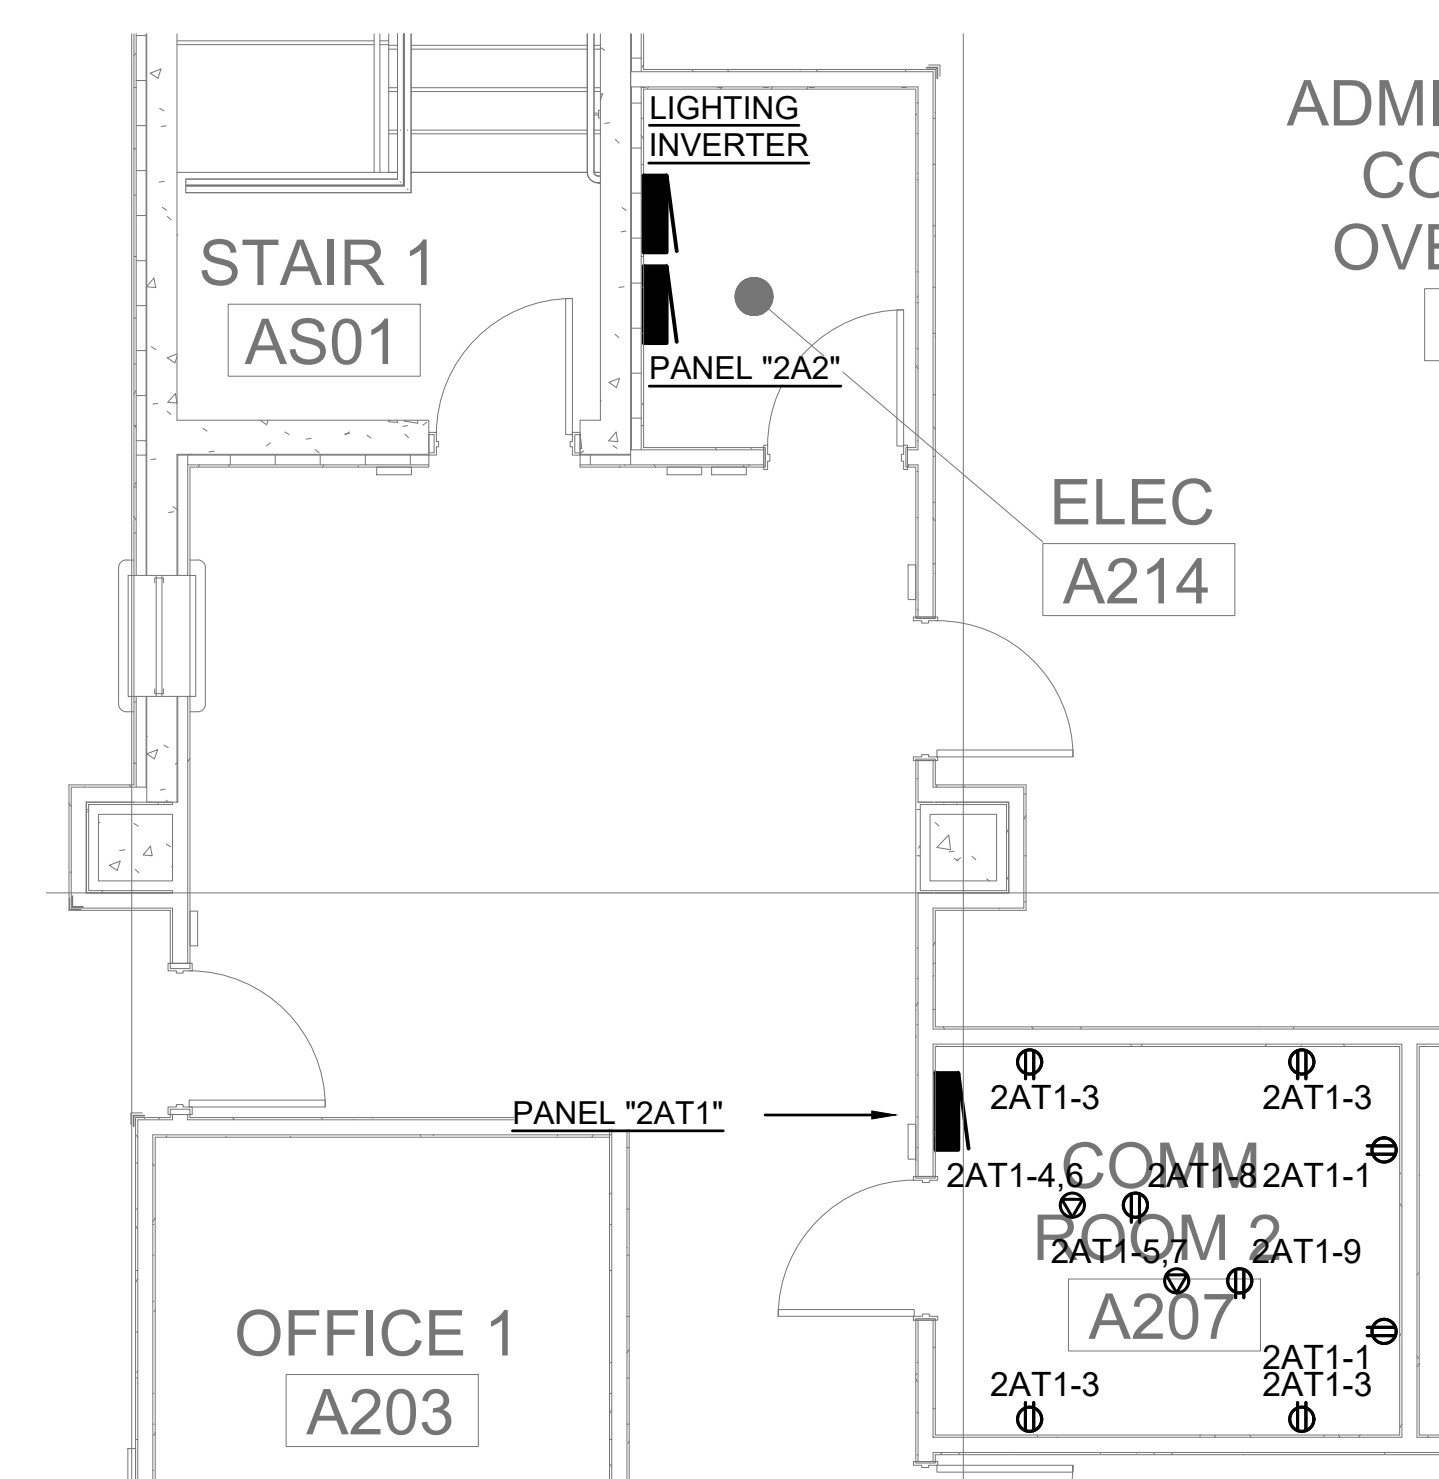

C11 2ND FLOOR ELEC AND COMM ROOM

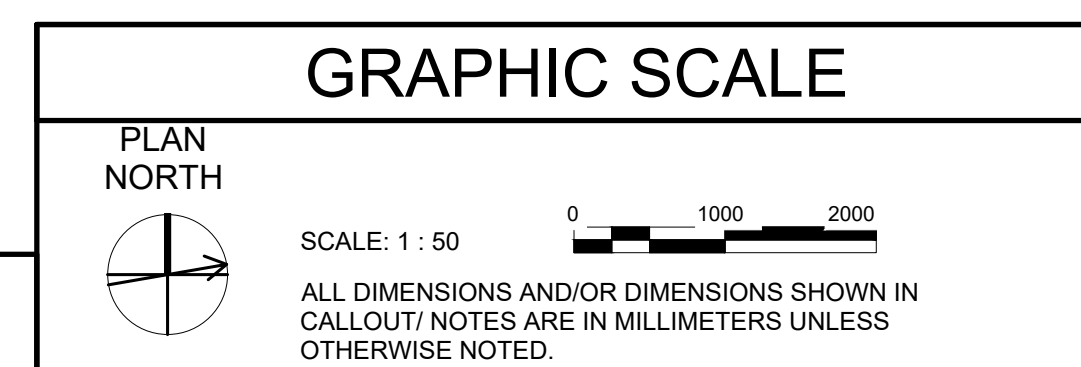

CLIN 0001

[illegible]


JAPAN DISTRICT, OKINAWA AREA OFFICE USAED-J, UNIT 35132 APO, AF 96374-5132	DRAWN BY:	SOLICITATION NO.:
	CHECKED BY:	CONTRACT NO.:
	SUBMITTED BY:	SCALE: AS SHOWN
	SIZE:	FILE NAME:

MADEIRA AIR BASE, OKINAWA, JAPAN
VEHICLE MAINTENANCE SHOP
FY20 MCA PN77833

VMS - ONE LINE DIAGRAM (CLIN 0001)

SHEET ID

EA601

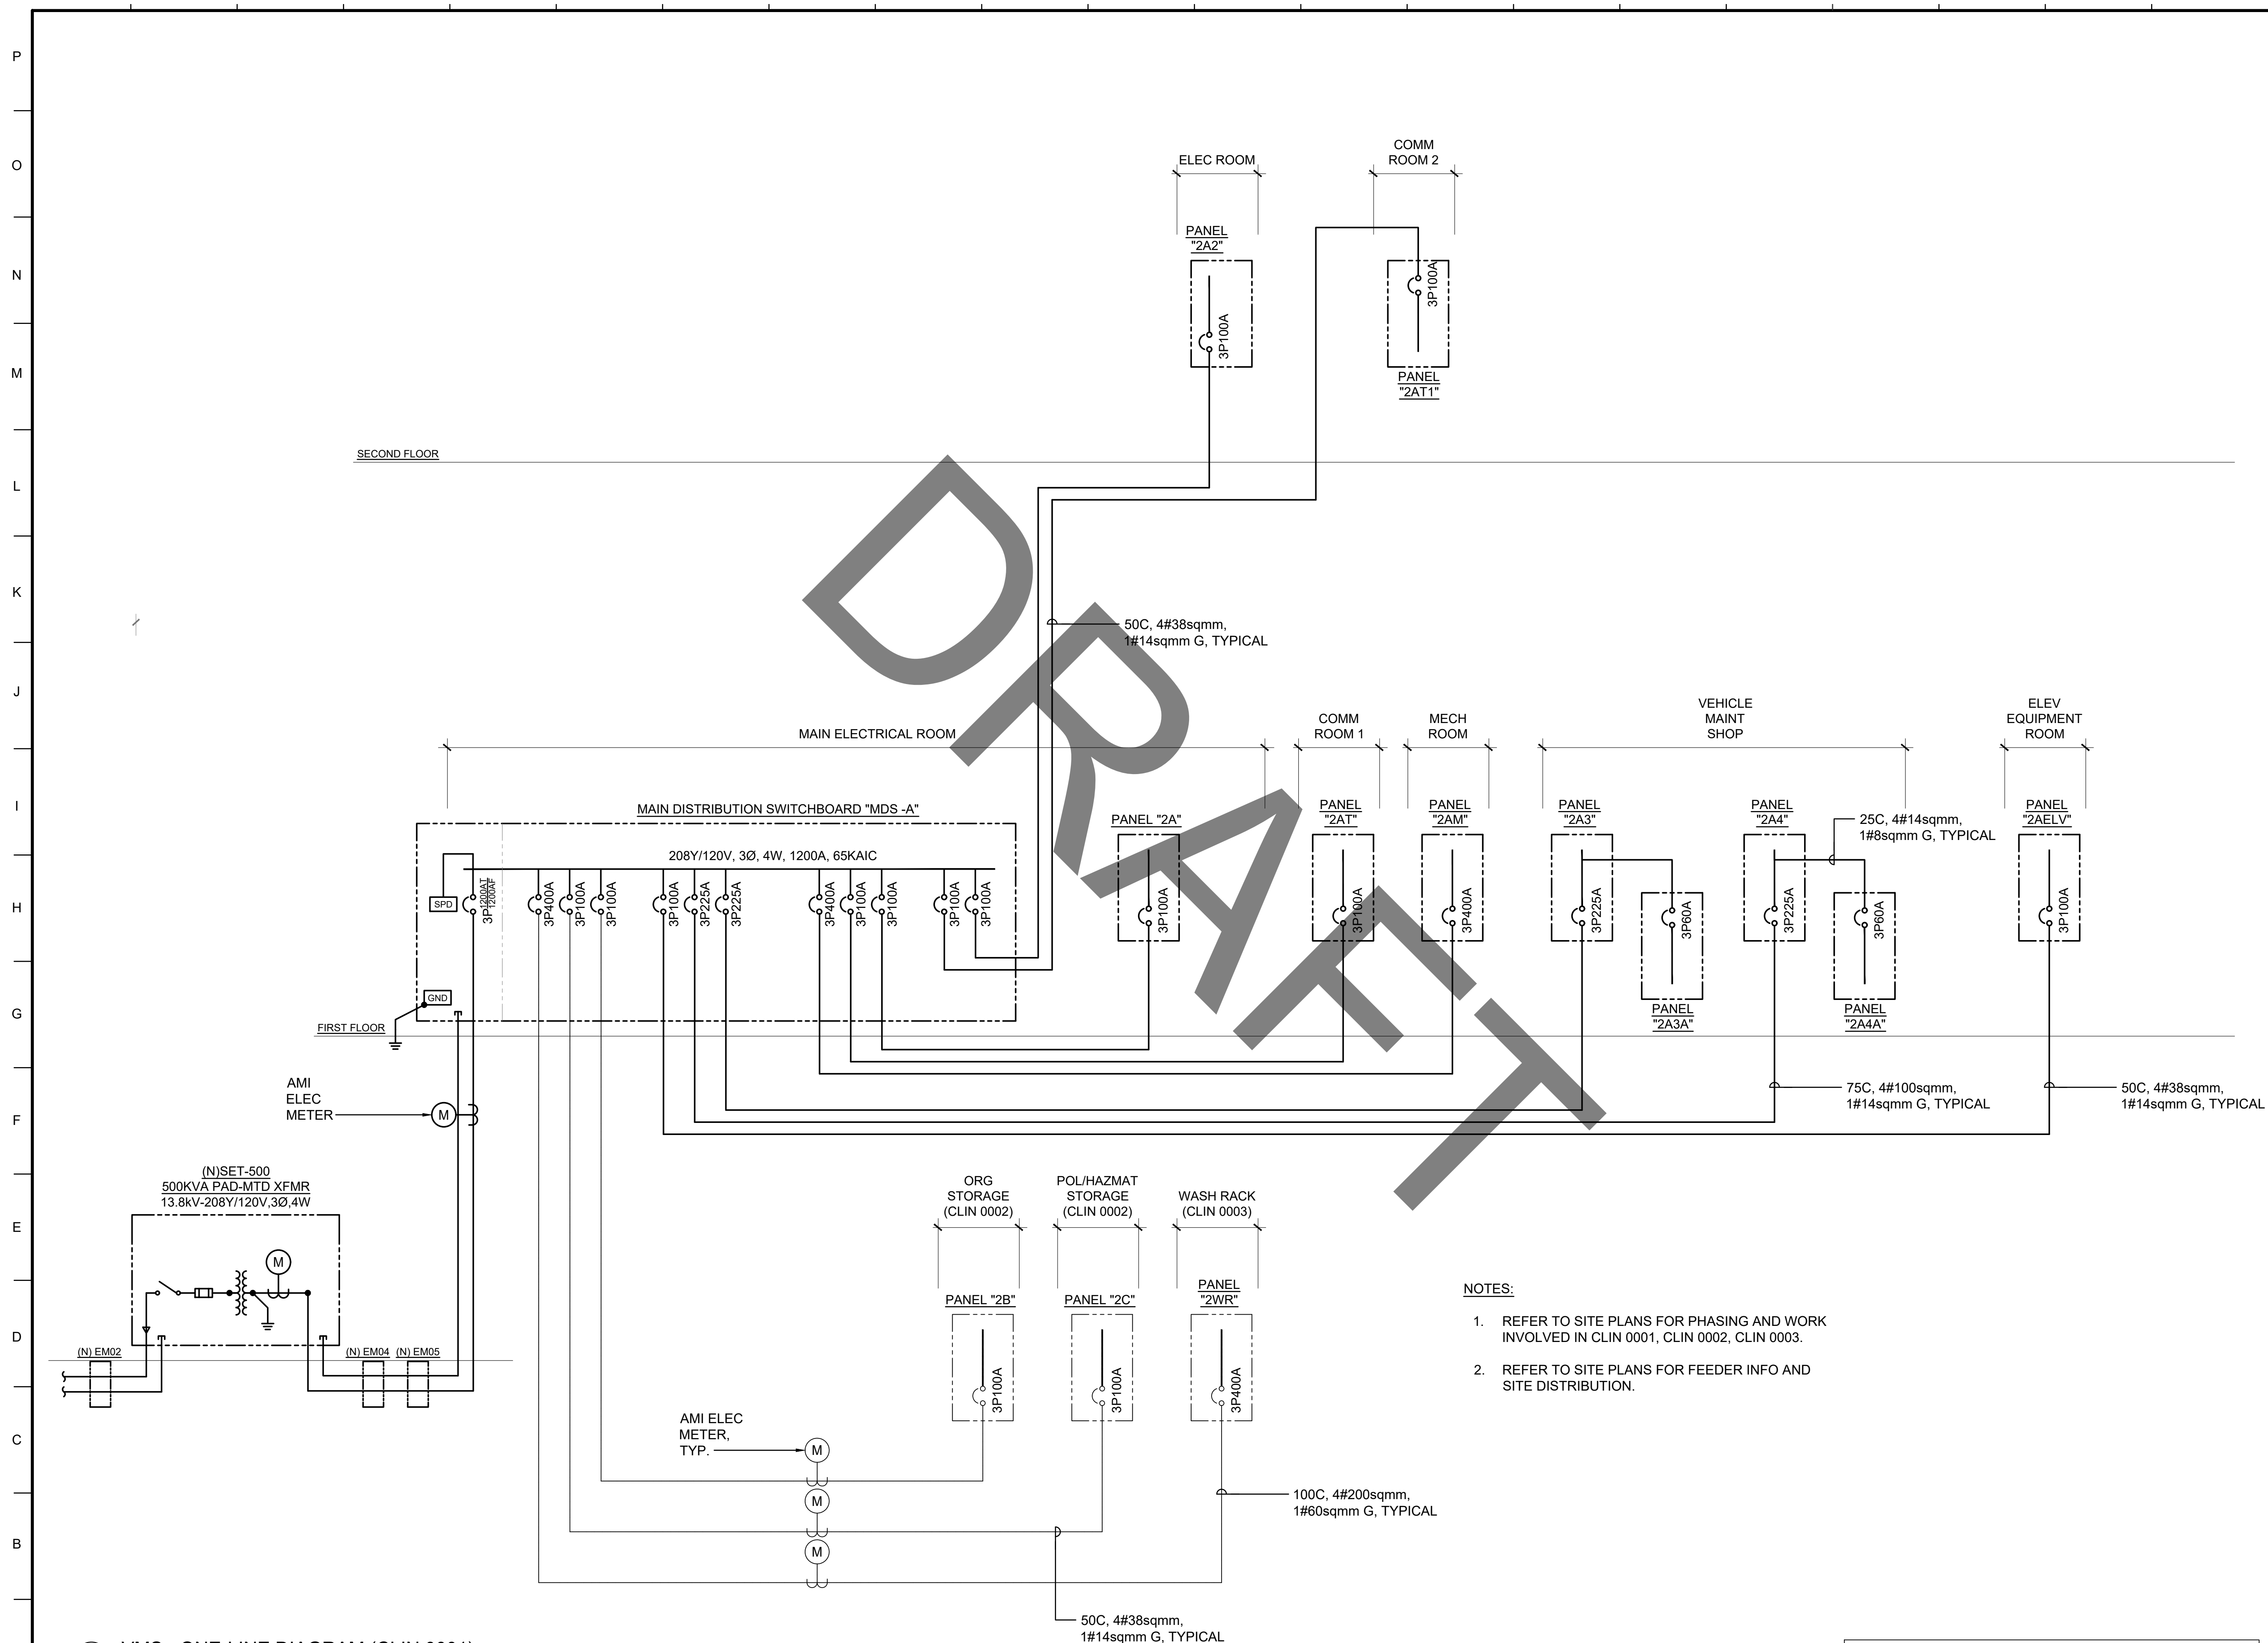

NOTES:

1. REFER TO SITE PLANS FOR PHASING AND WORK INVOLVED IN CLIN 0001, CLIN 0002, CLIN 0003.
2. REFER TO SITE PLANS FOR FEEDER INFO AND SITE DISTRIBUTION.

CLIN 0001-0003

INTERMEDIATE DESIGN

OS - POWER PLAN (CLIN 0002)

1:100

[illegible]

US ARMY CORPS OF ENGINEERS JAPAN DISTRICT, OKINAWA AREA OFFICE U.S. ARMY BOX 35152 APO, AP 96374-0152	DESIGNED BY: DRAWN BY: CHECKED BY: SUBMITTED BY: SIZE:	ISSUE DATE: SOLICITATION NO.: CONTRACT NO.: SCALE: FILE NAME:
 SOFM INTERNATIONAL, INC. 501 SUMNER STREET, SUITE 620		


KADENA AIR BASE, OKINAWA, JAPAN
VEHICLE MAINTENANCE SHOP
FY20 MCA PN77833

OS - ONE LINE DIAGRAM (CLIN 0002)

SHEET ID

EB601

INTERMEDIATE DESIGN

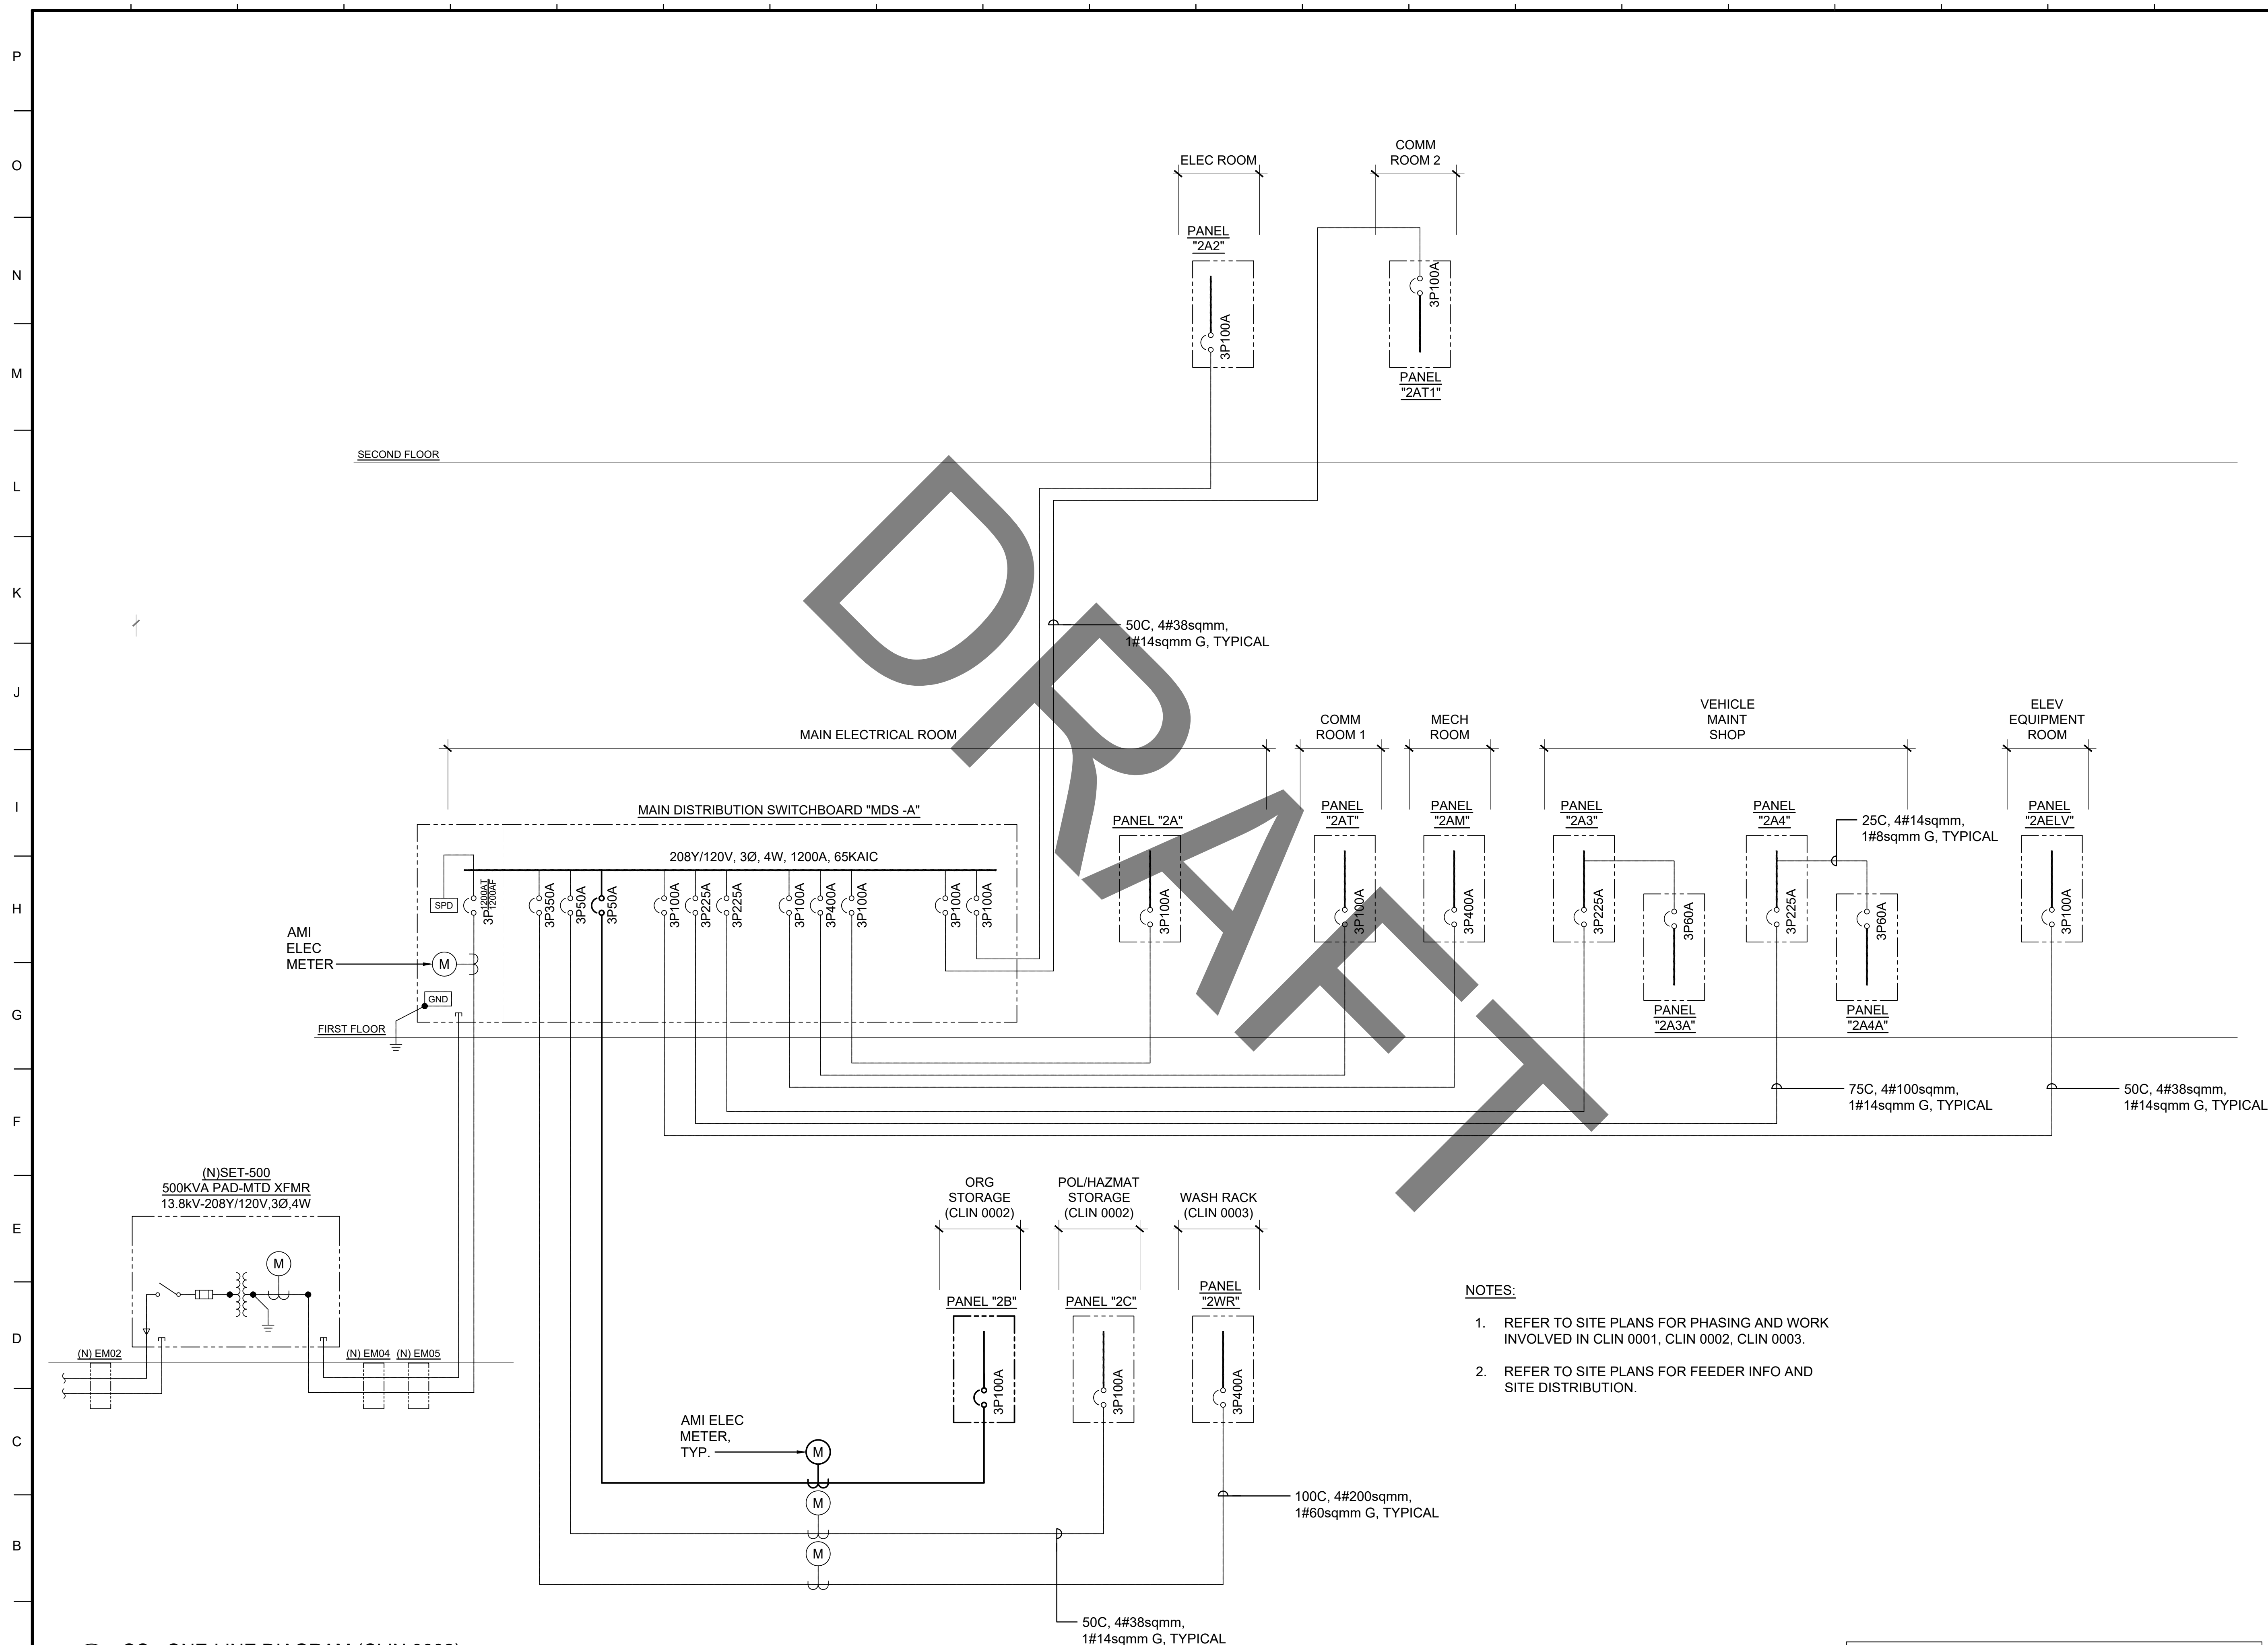

CLIN 0002

A1 OS - ONE-LINE DIAGRAM (CLIN 0002)
NONE

[illegible]


JAPAN DISTRICT, OKINAWA AREA OFFICE USAED-J, UNIT 35132 APO, AP 96374-5132	DRAWN BY: CHECKED BY: SUBMITTED BY: SCALE: AS SHOWN	SOLICITATION NO.: CONTRACT NO.:
 SSFM INTERNATIONAL, INC 501 SUMNER STREET, SUITE 620	SIZE: FILE NAME:	

MADEIRA AIR BASE, GUINAWA, JAPAN
VEHICLE MAINTENANCE SHOP
FY20 MCA PN77833


SHEET ID

EC101


INTERMEDIATE DESIGN

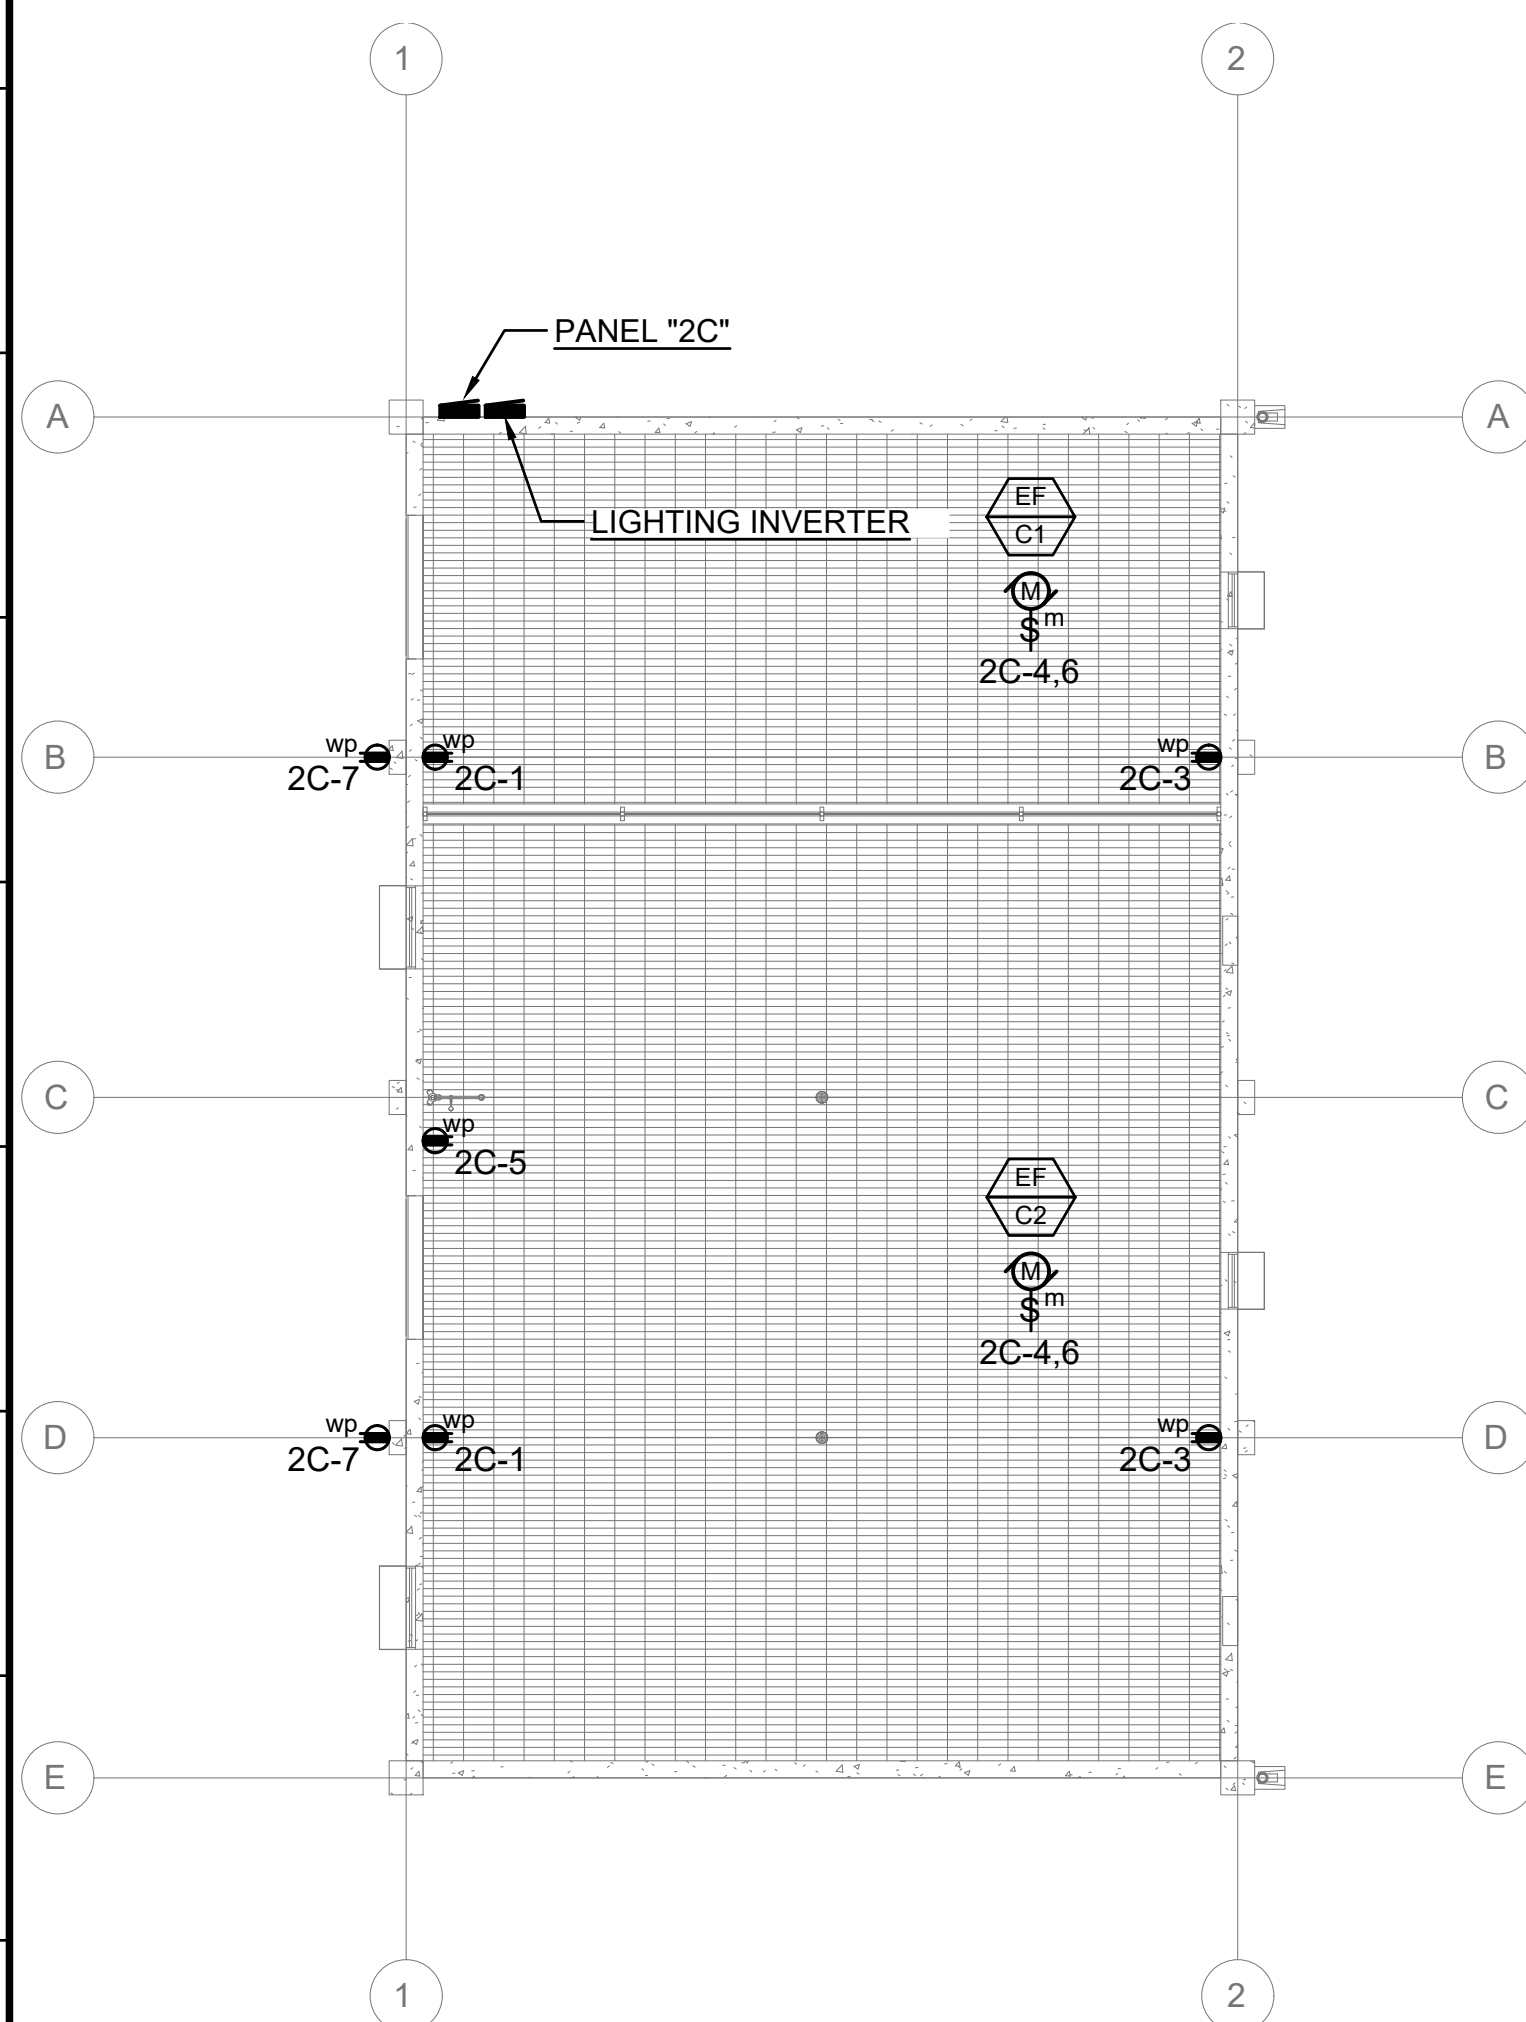


B1 POL & HAZMAT - POWER PLAN (CLIN 0002)
1:100

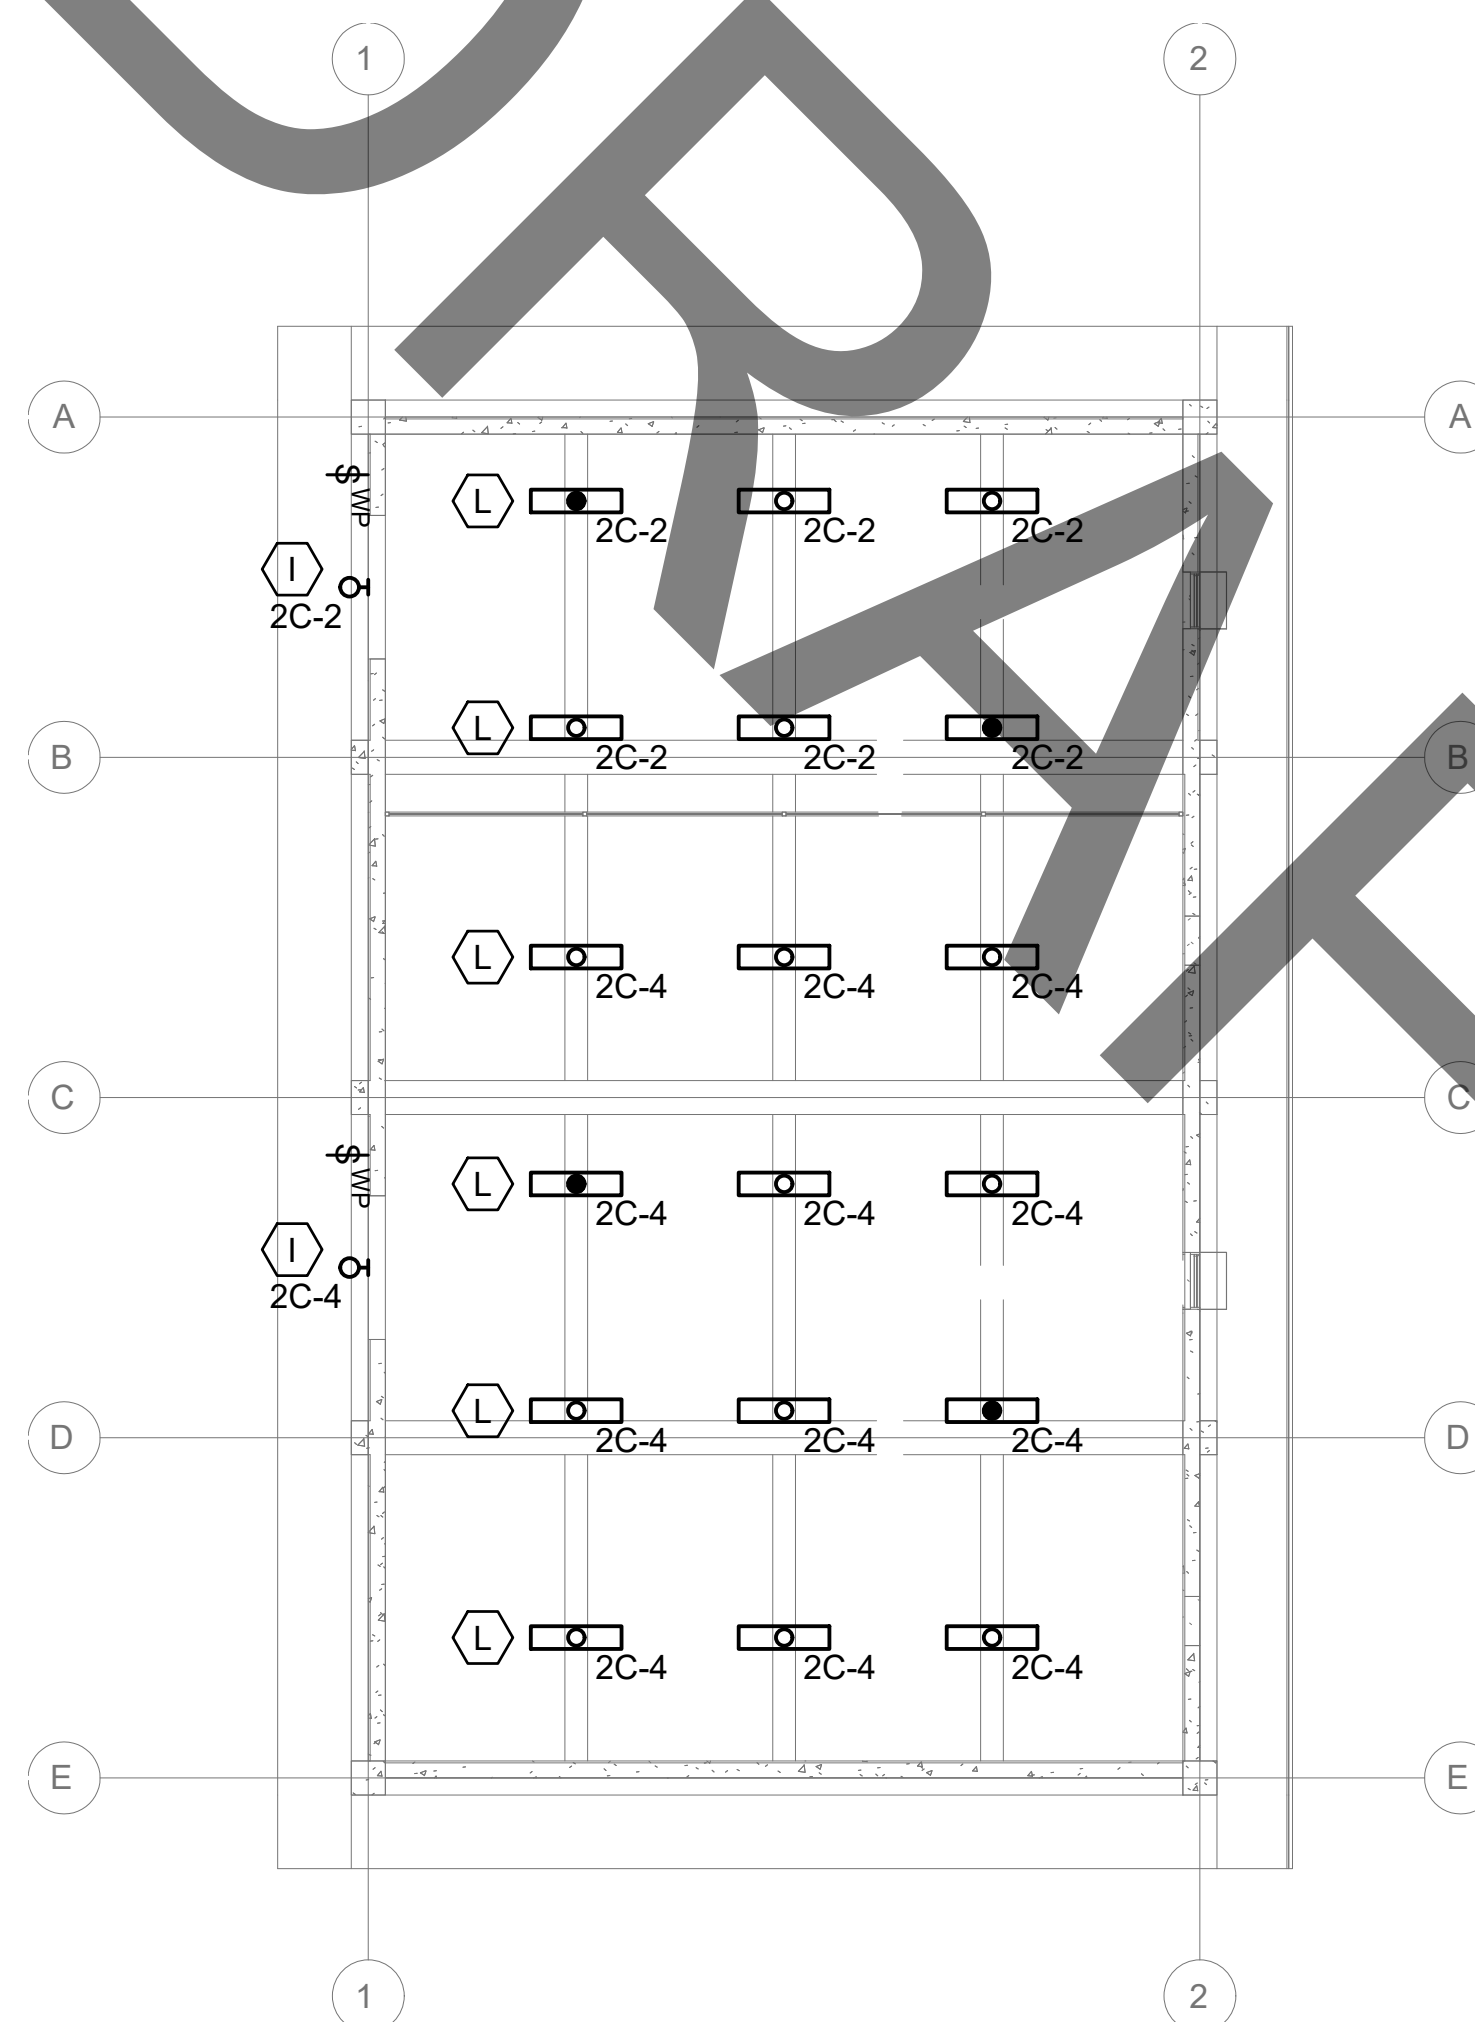

B8 POL & HAZMAT - LIGHTING PLAN (CLIN 0002)
1:100

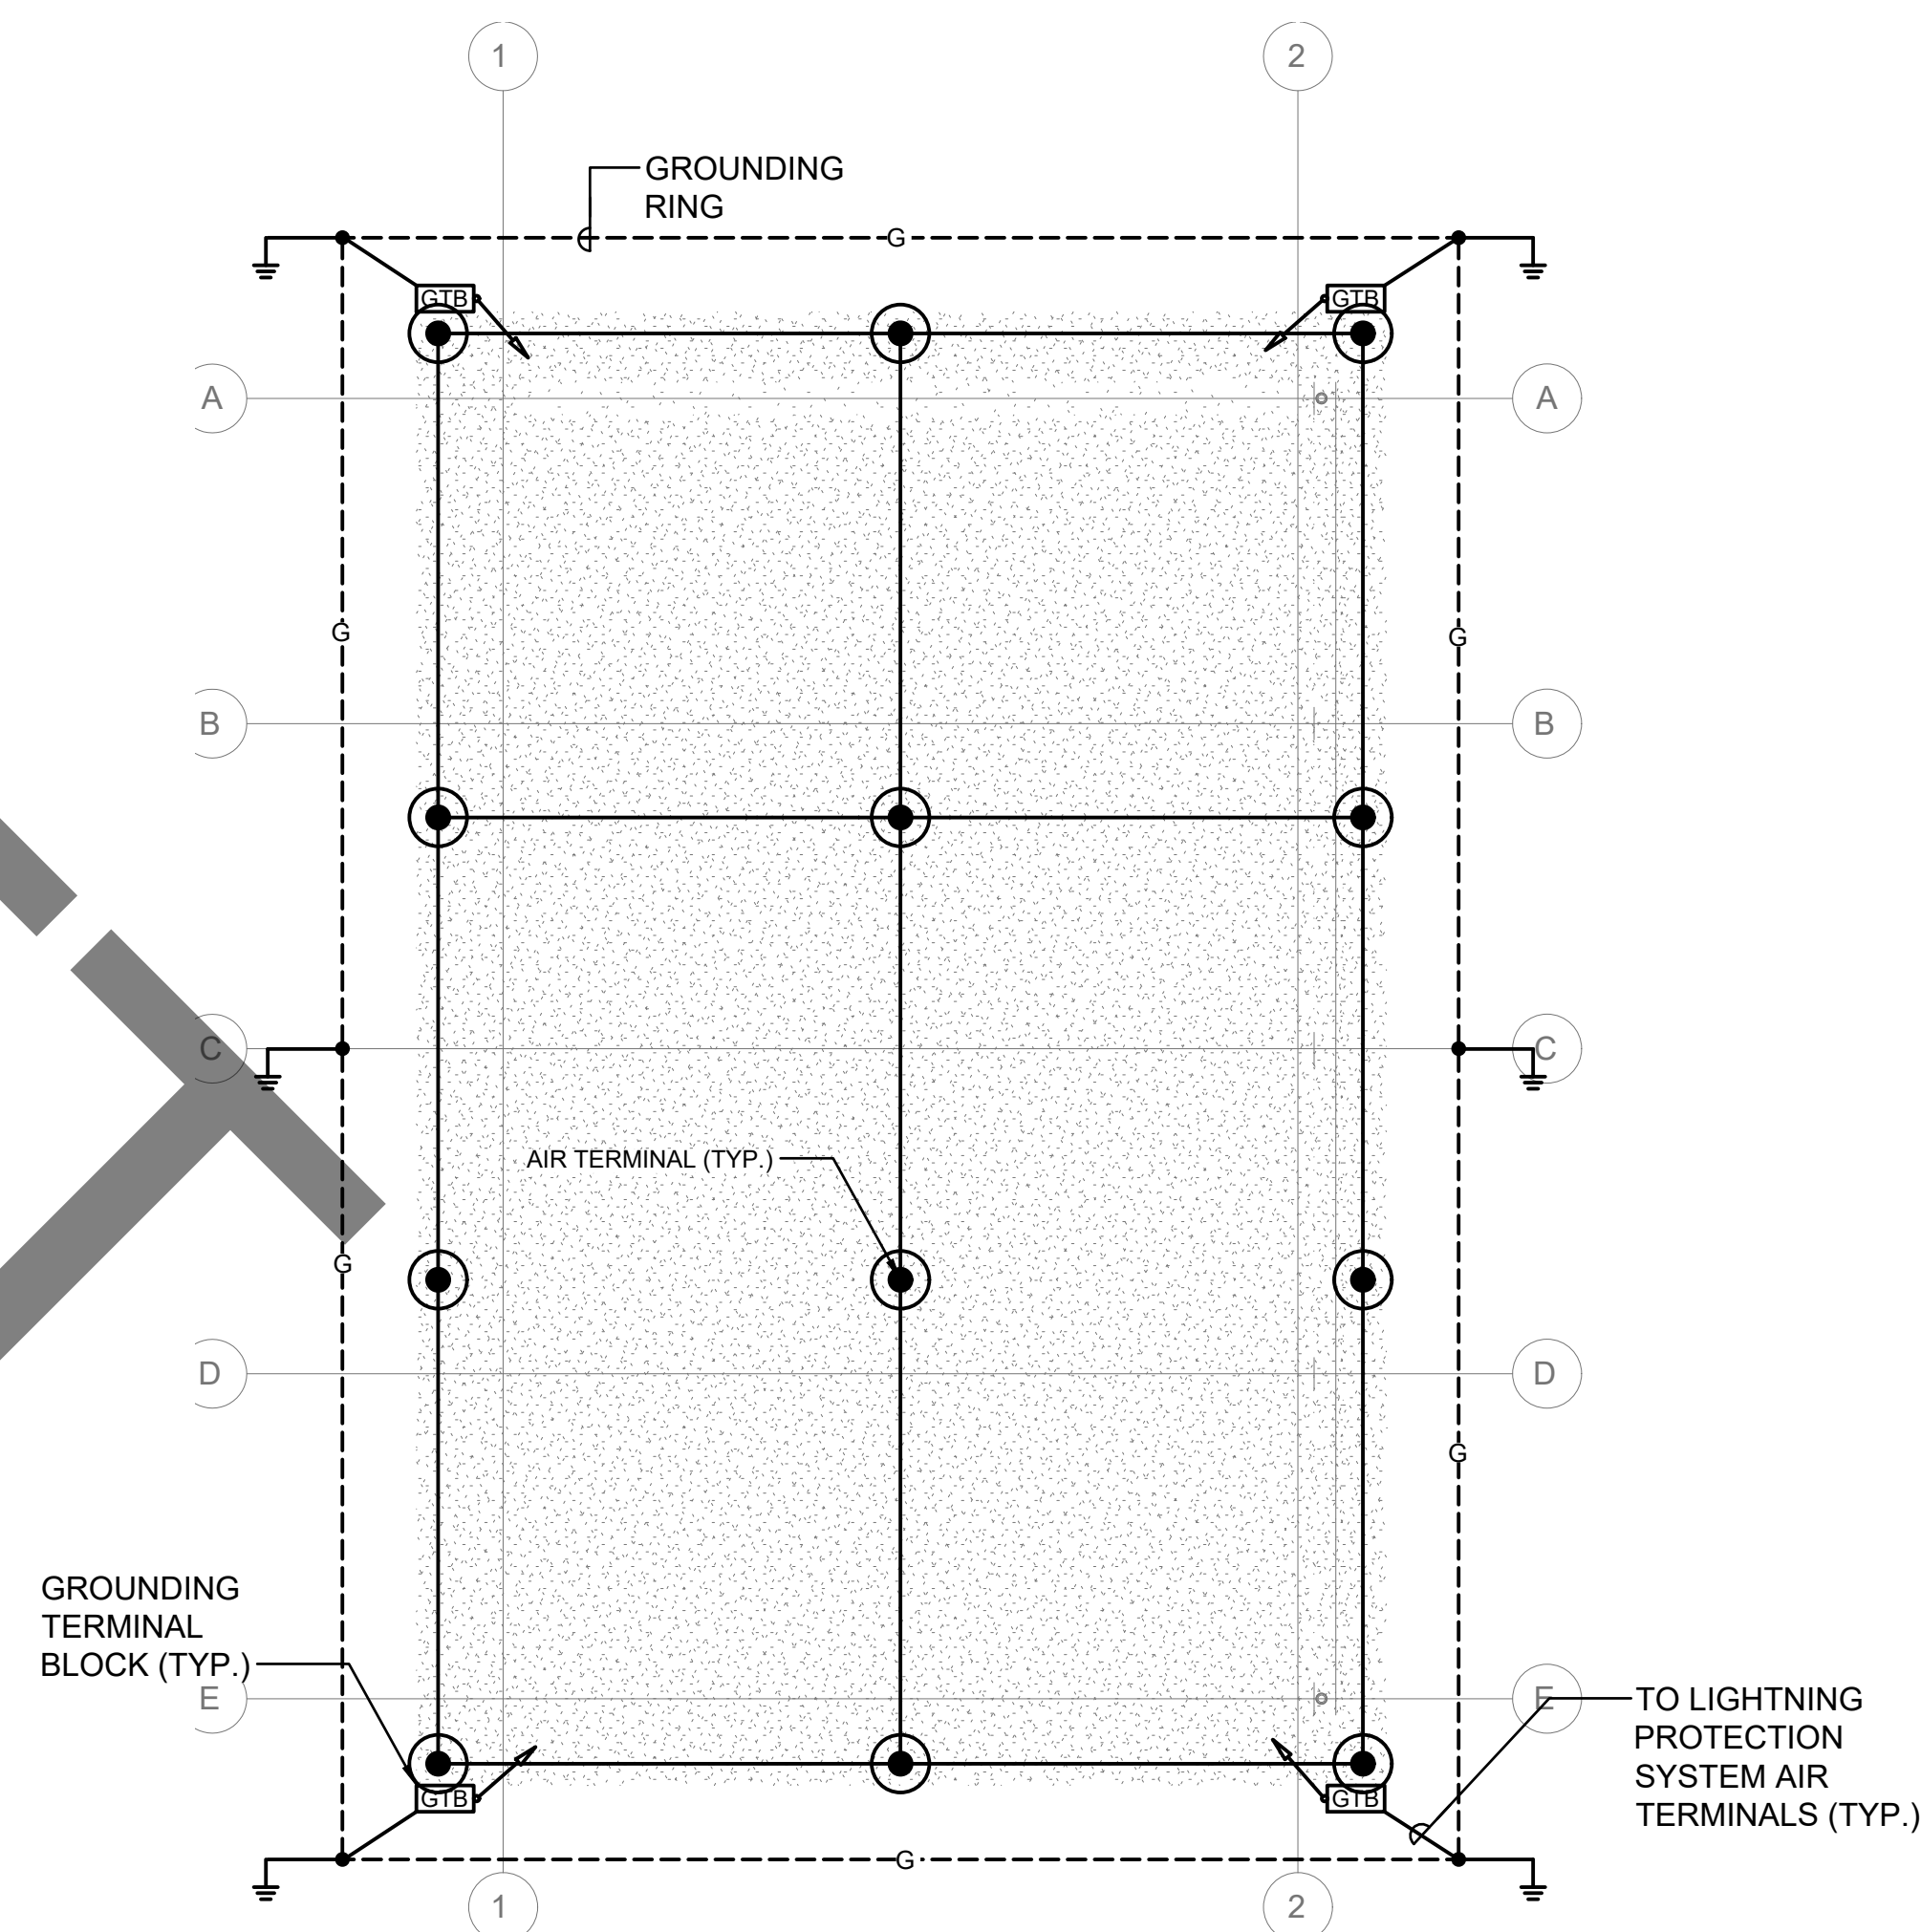

B15 POL & HAZMAT - LIGHTNING PROTECTION PLAN

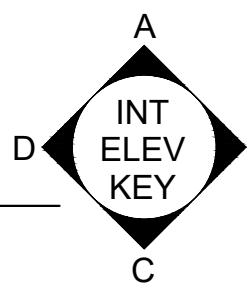

GRAPHIC SCALE



SCALE: 1 : 100

ALL DIMENSIONS AND/OR DIMENSIONS SHOWN IN
CALLOUT/ NOTES ARE IN MILLIMETERS UNLESS
OTHERWISE NOTED.

CLIN 0002

[illegible]


JAPAN DISTRICT, OKINAWA AREA OFFICE USAED-J, UNIT 35132 APO, AF 96374-5132	DRAWN BY:	SOLICITATION NO.:
	CHECKED BY:	CONTRACT NO.:
	SUBMITTED BY:	SCALE: AS SHOWN
	SIZE:	FILE NAME:


POL & HAZMAT - ONE LINE DIAGRAM (CLIN 0002)

SHEET ID

EC601


INTERMEDIATE DESIGN

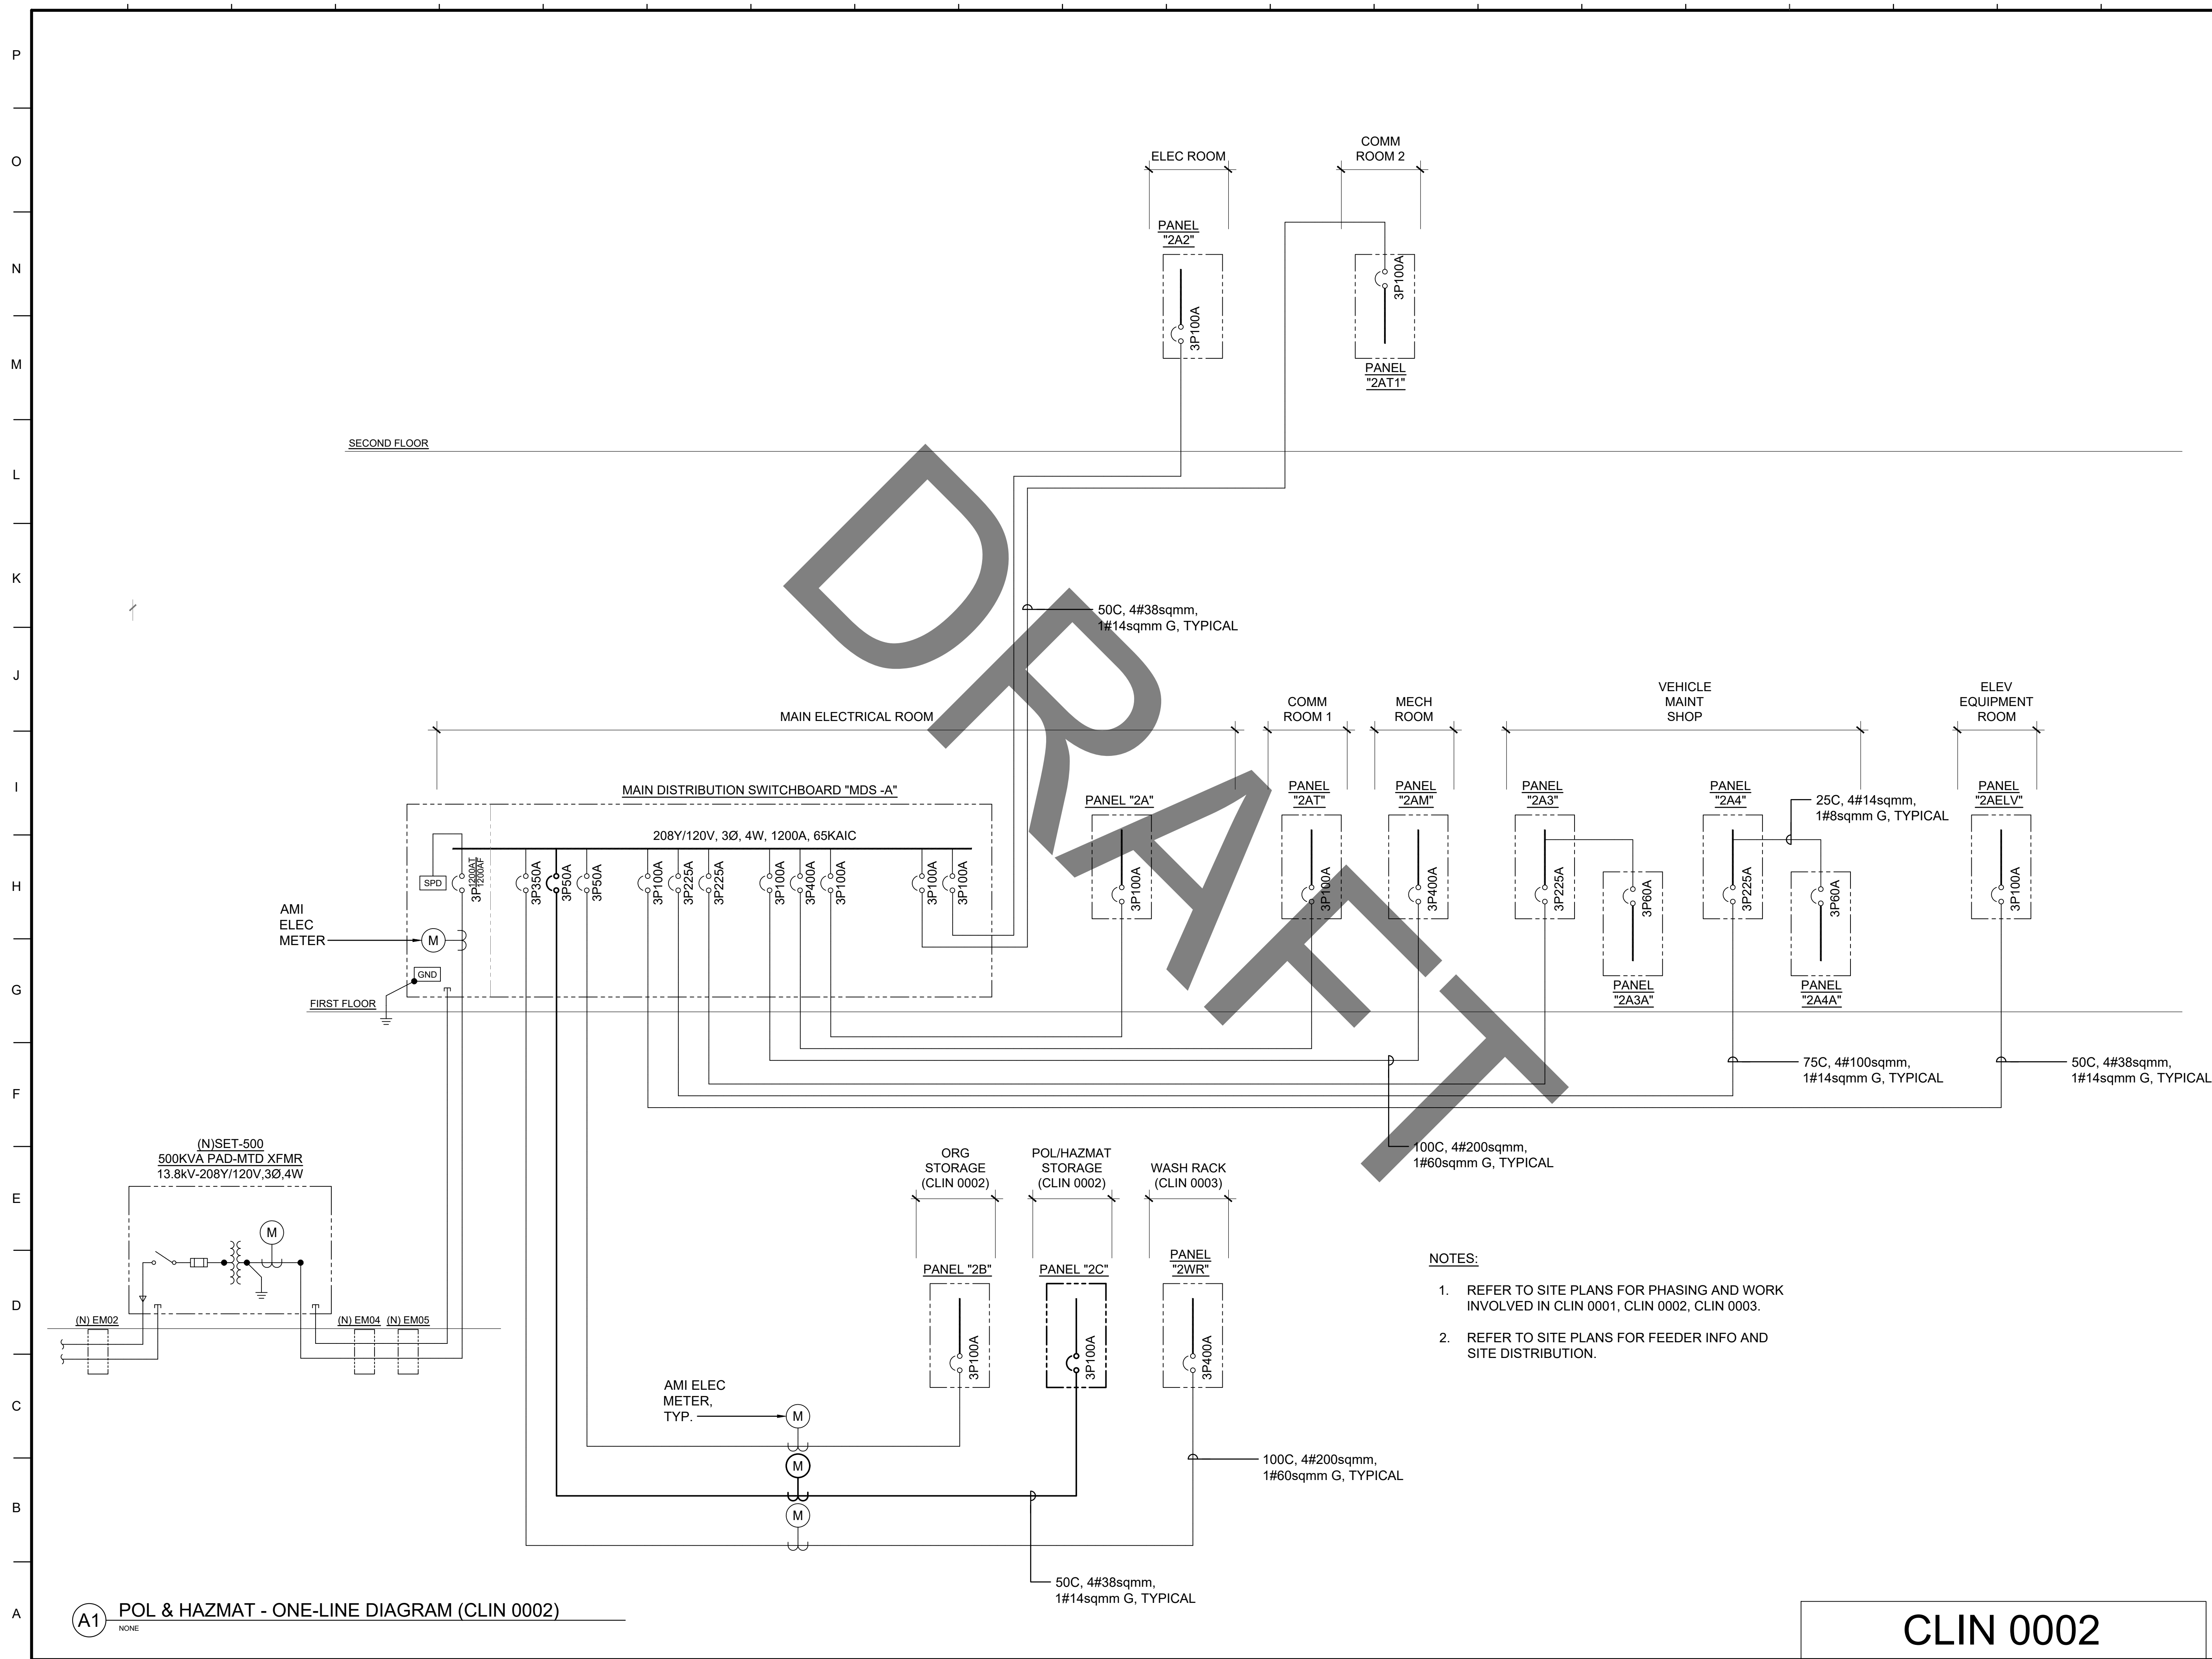

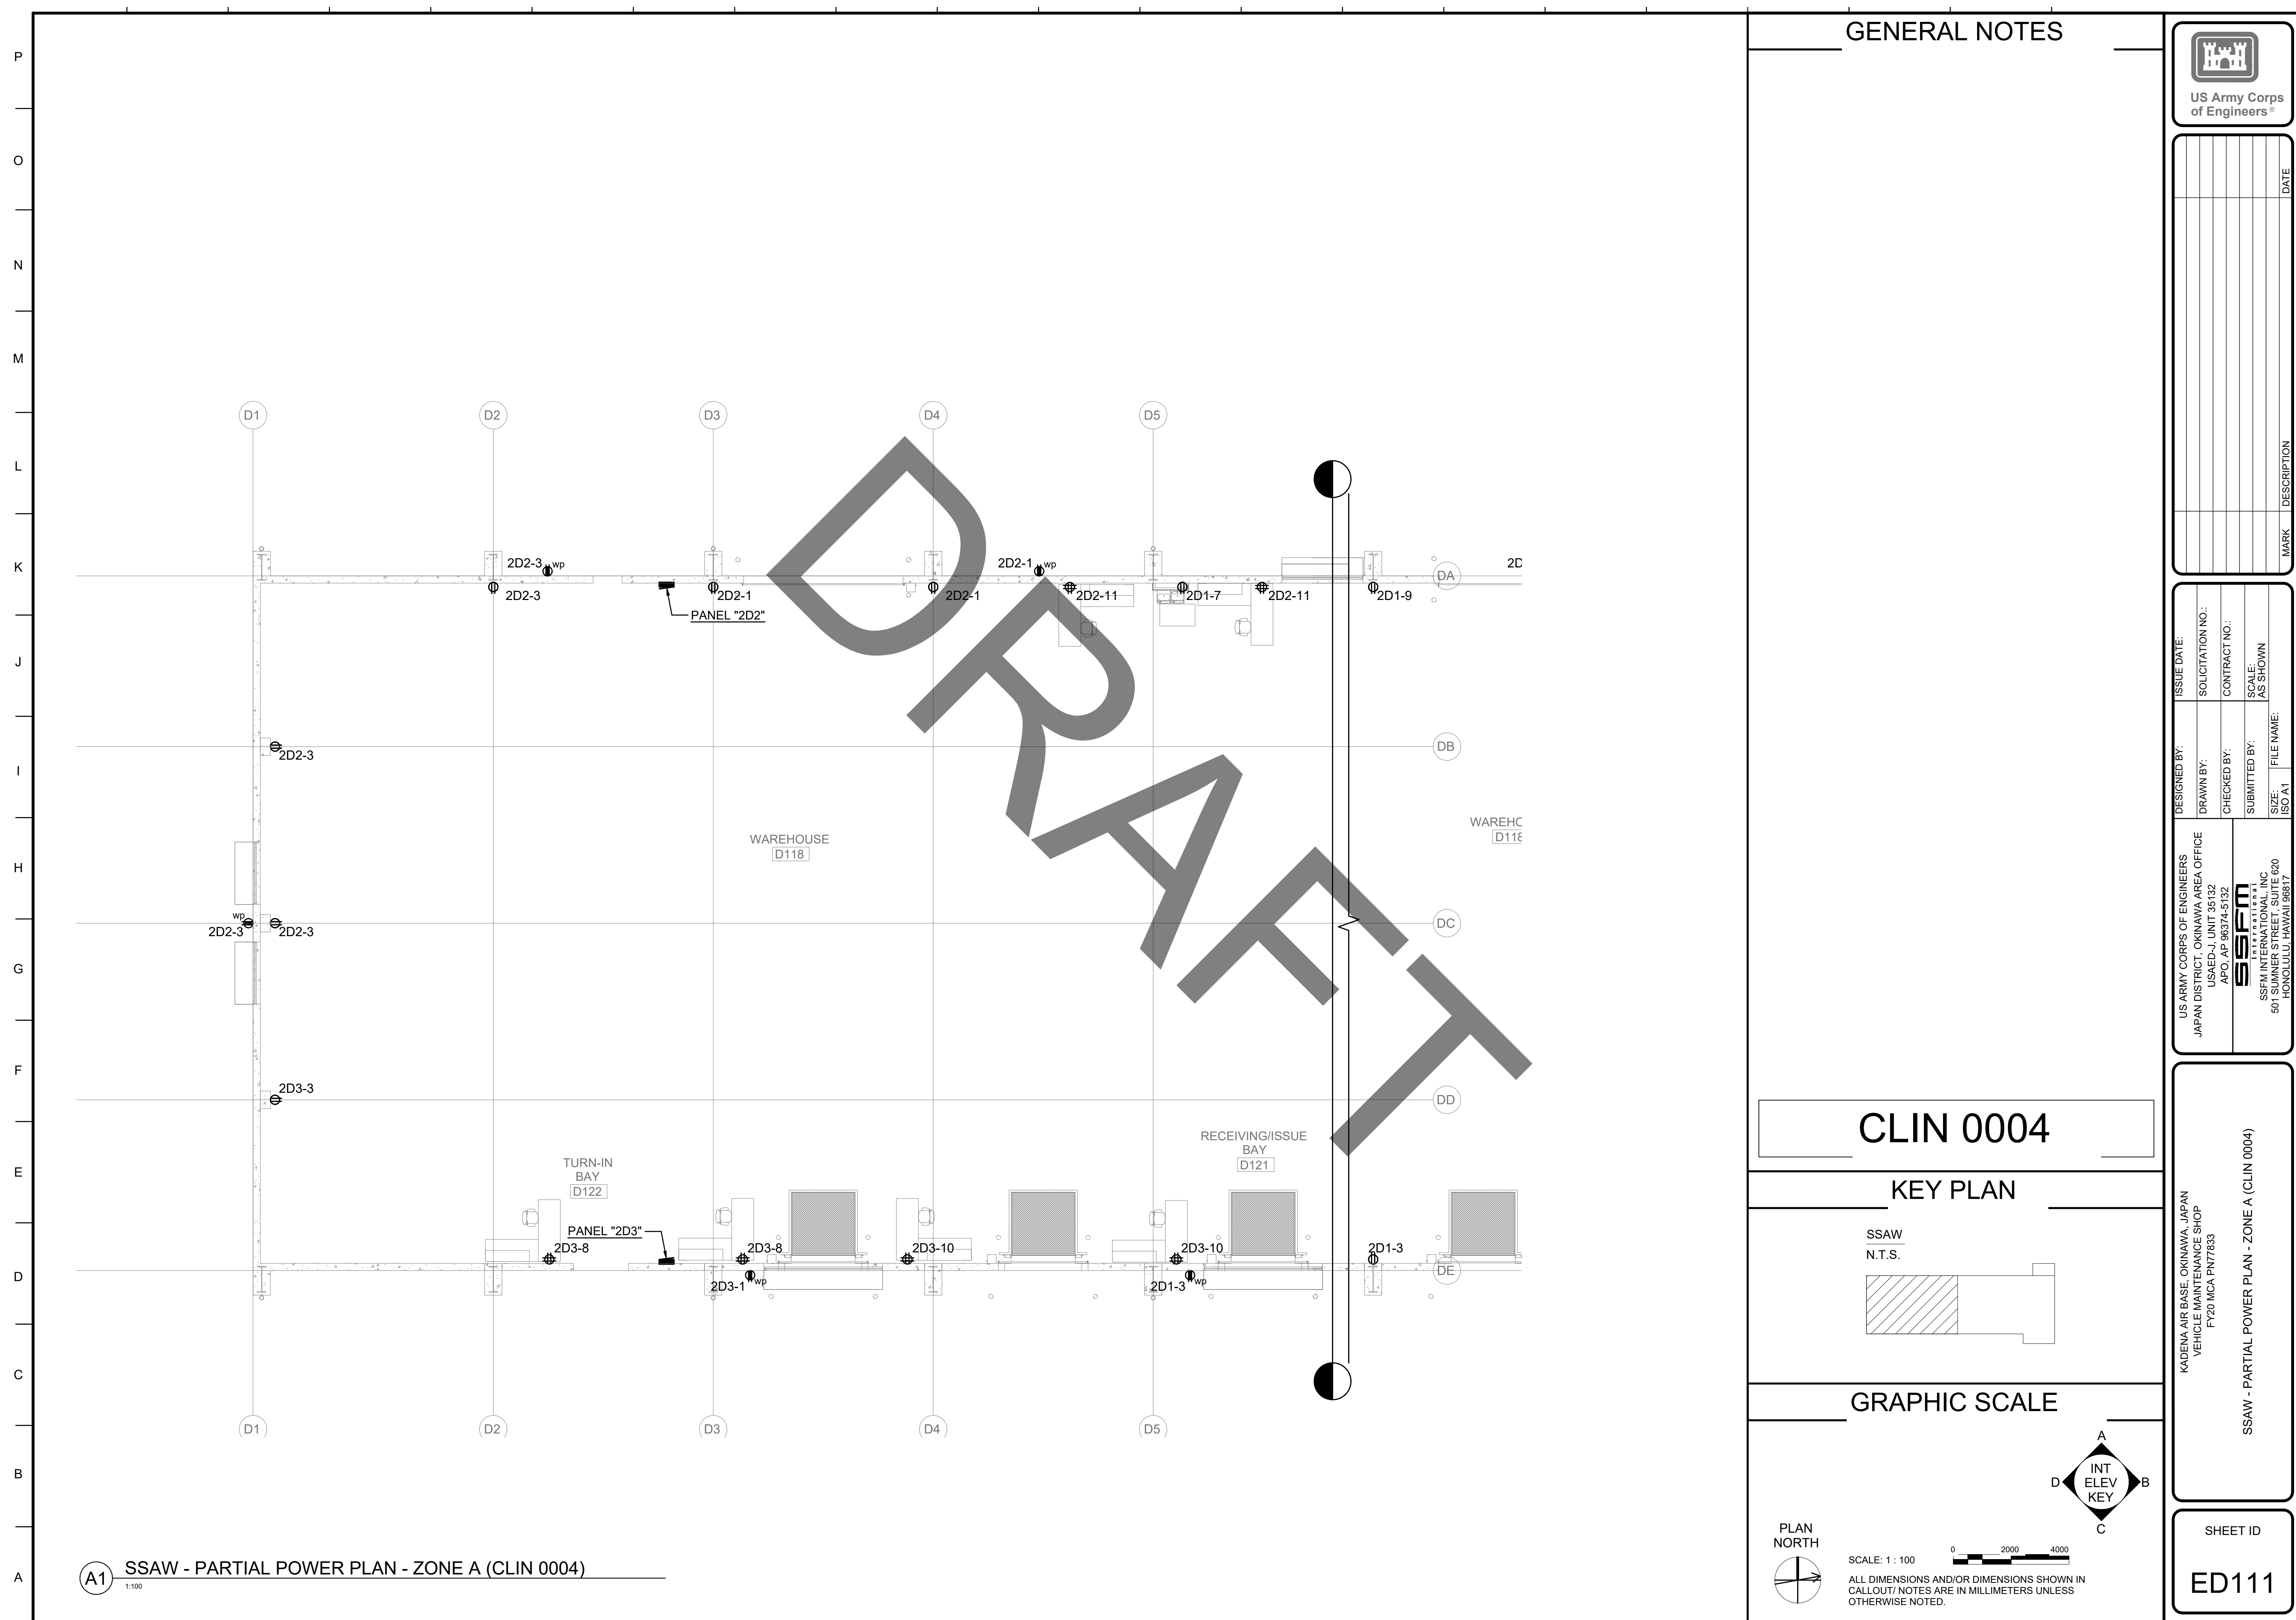

A1 SS

— P
— O
— N
— M
— L
— K
— J
— I
— H
— G
— F
— E
— D
— C
— B
— A

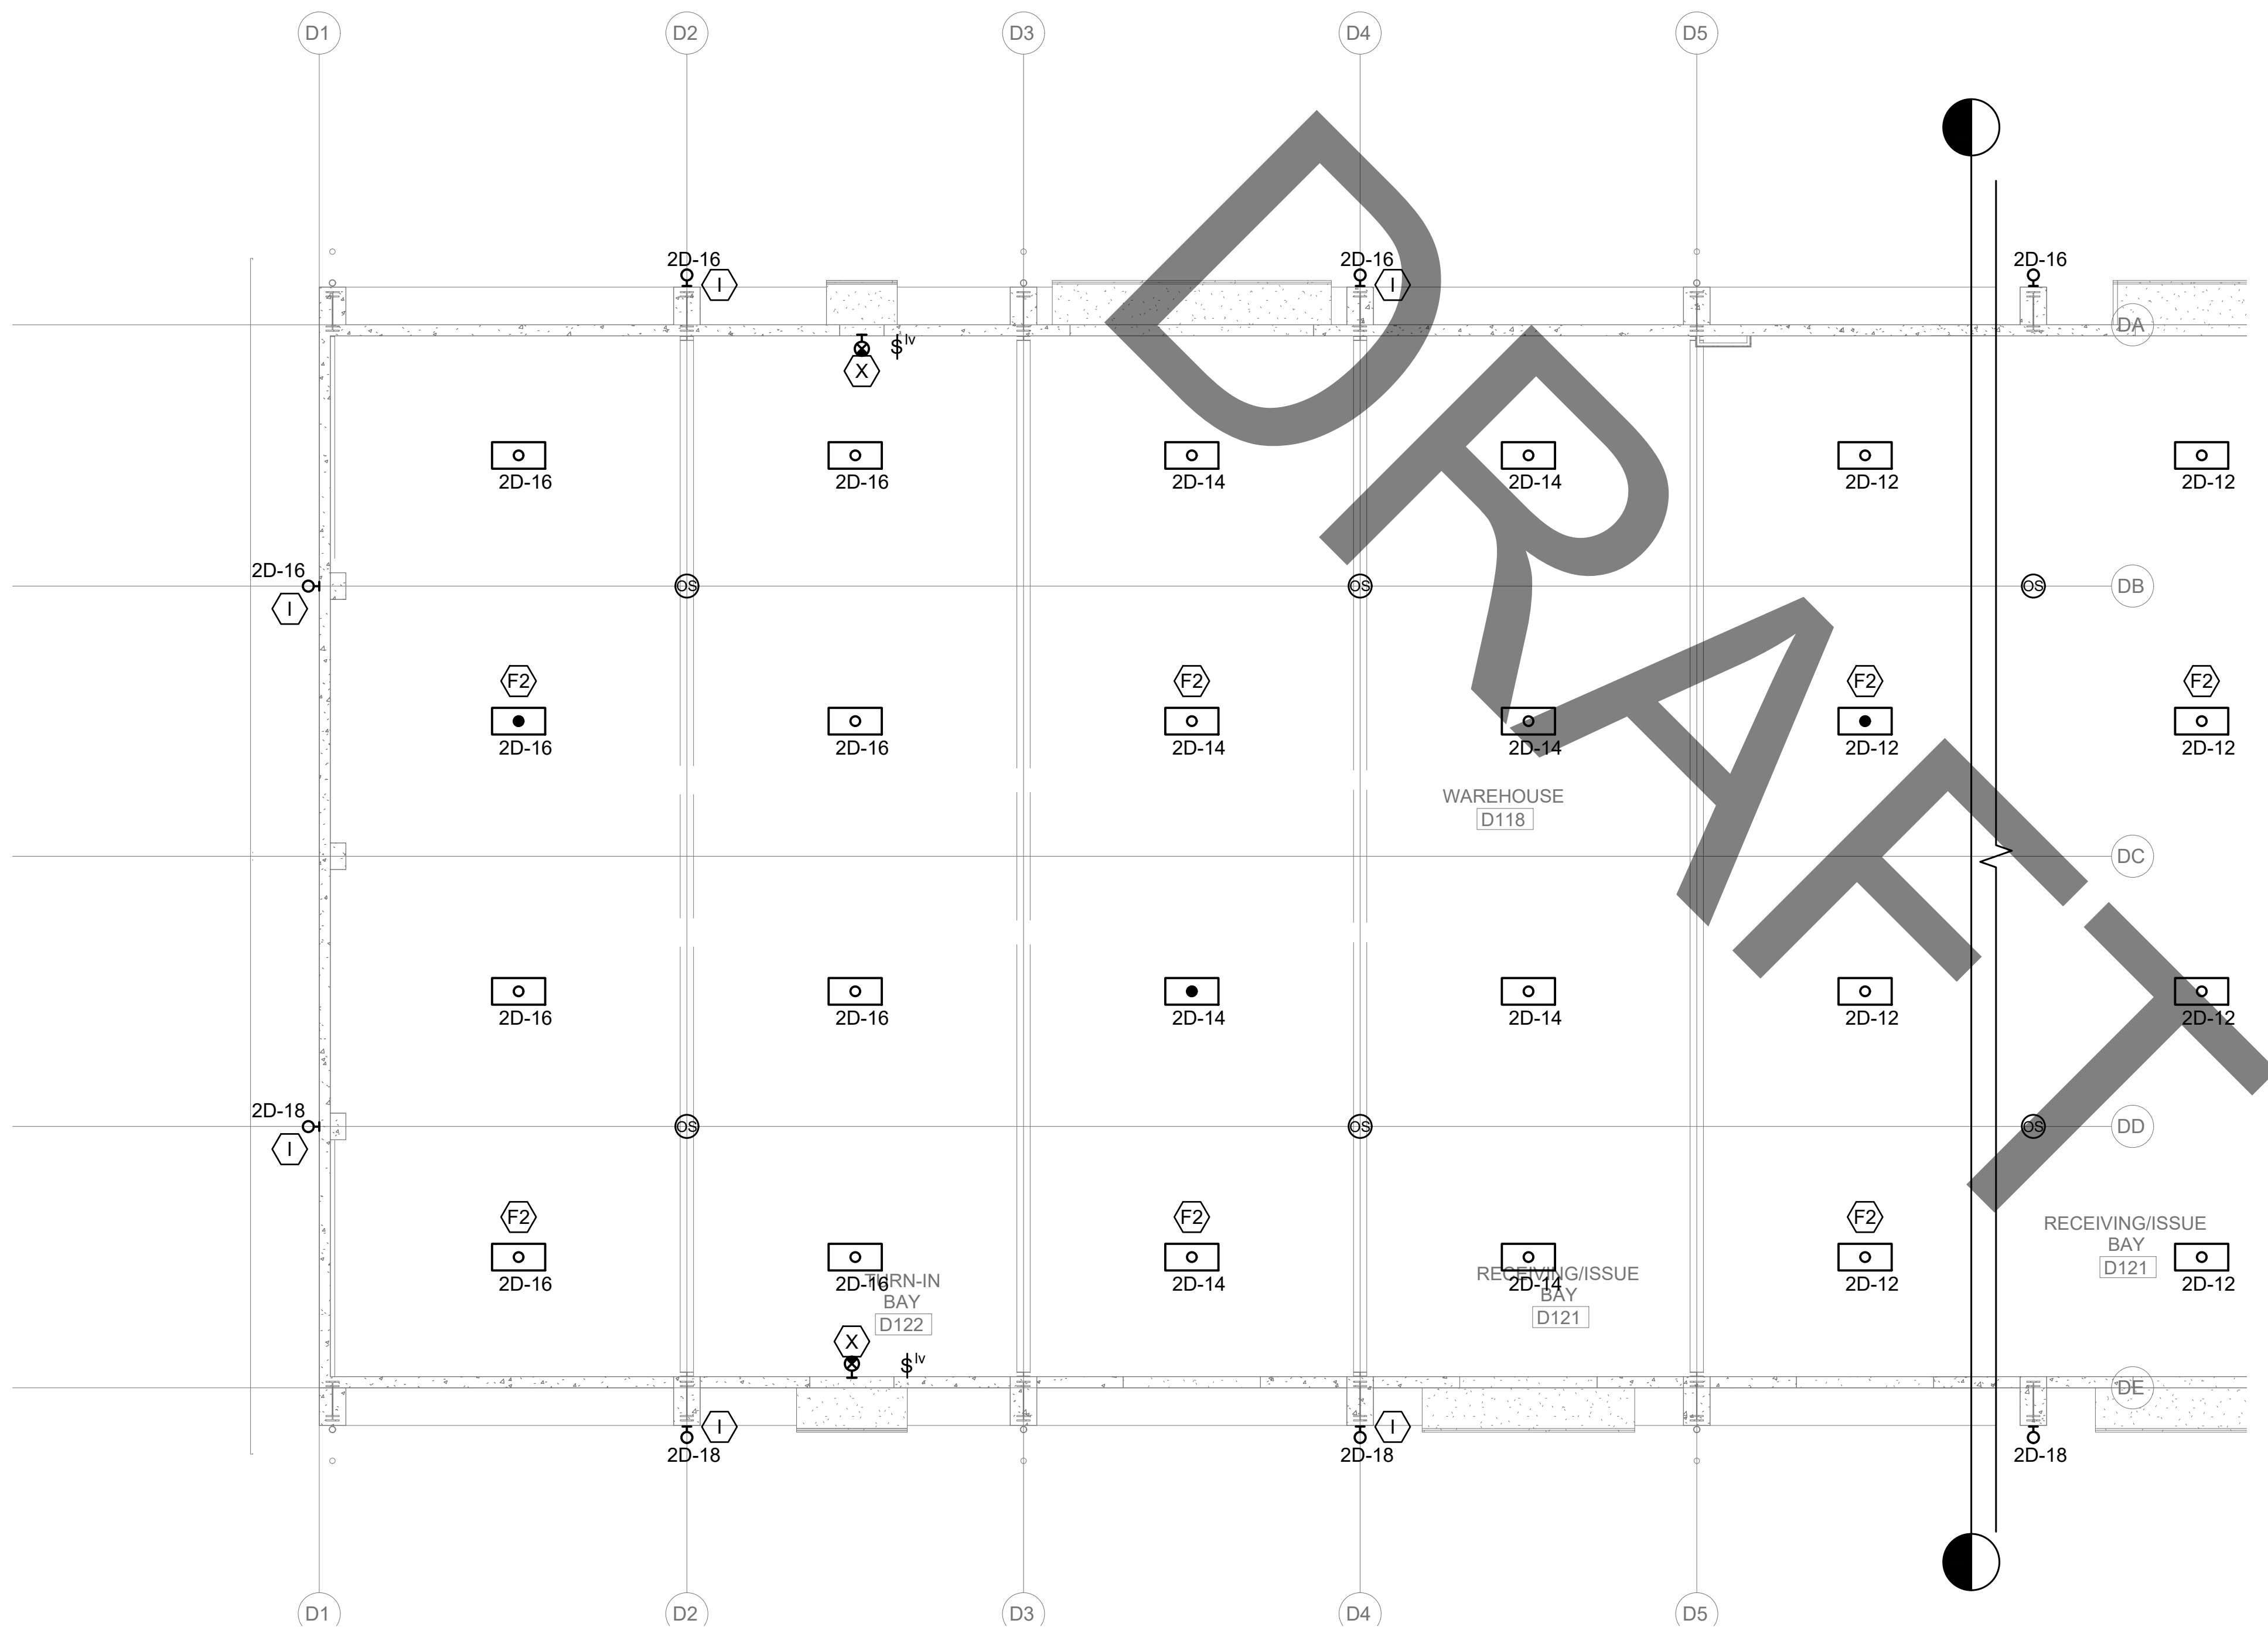

A1 **SSAW - PARTIAL LIGHTING PLAN - ZONE A (CLIN 0004)**
1:100

GENERAL NOTES

US Army Corps
of Engineers®

LEGEND

[illegible]

DESIGNED BY:	ISSUE DATE:
DRAWN BY:	SOLICITATION NO.:
CHECKED BY:	CONTRACT NO.:
SUBMITTED BY:	SCALE: AS SHOWN
FILE NAME:	

US ARMY CORPS OF ENGINEERS
JAPAN DISTRICT, OKINAWA AREA OFFICE
USAE-J, UNIT 35132
APO, AP 96374-5132

USACE

SSFM INTERNATIONAL, INC
501 SUMNER STREET, SUITE 620
SOFM

KADENA AIR BASE, OKINAWA, JAPAN
VEHICLE MAINTENANCE SHOP
FY20 MCA PN77833


SHEET ID

ED121

INTERMEDIATE DESIGN

CLIN 0004


KEY PLAN

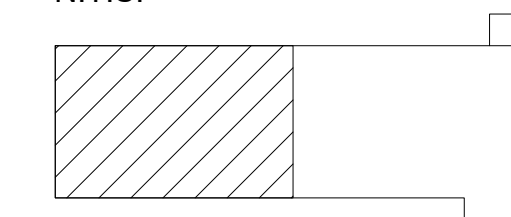SSAW
N.T.S.


GRAPHIC SCALE



SCALE: 1 : 100

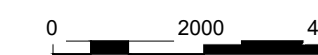

ALL DIMENSIONS AND/OR DIMENSIONS SHOWN IN
CALLOUT/ NOTES ARE IN MILLIMETERS UNLESS
OTHERWISE NOTED.

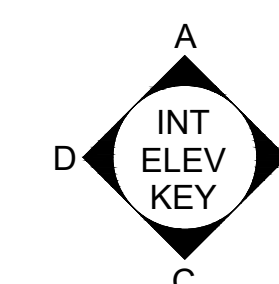

US Army Corps
of Engineers®

...	...
-----	-----

DESIGNED BY:	ISSUE DATE:
DRAWN BY:	SOLICITATION NO.:
CHECKED BY:	CONTRACT NO.:
SUBMITTED BY:	SCALE: AS SHOWN
SIZE:	FILE NAME:


SSFM International
SSFM INTERNATIONAL, INC.
401 SUMNER STREET, SUITE 620

KADENA AIR BASE, OKINAWA, JAPAN
VEHICLE MAINTENANCE SHOP
FY20 MCA PN77833

SHEET ID

ED122

INTERMEDIATE DESIGN

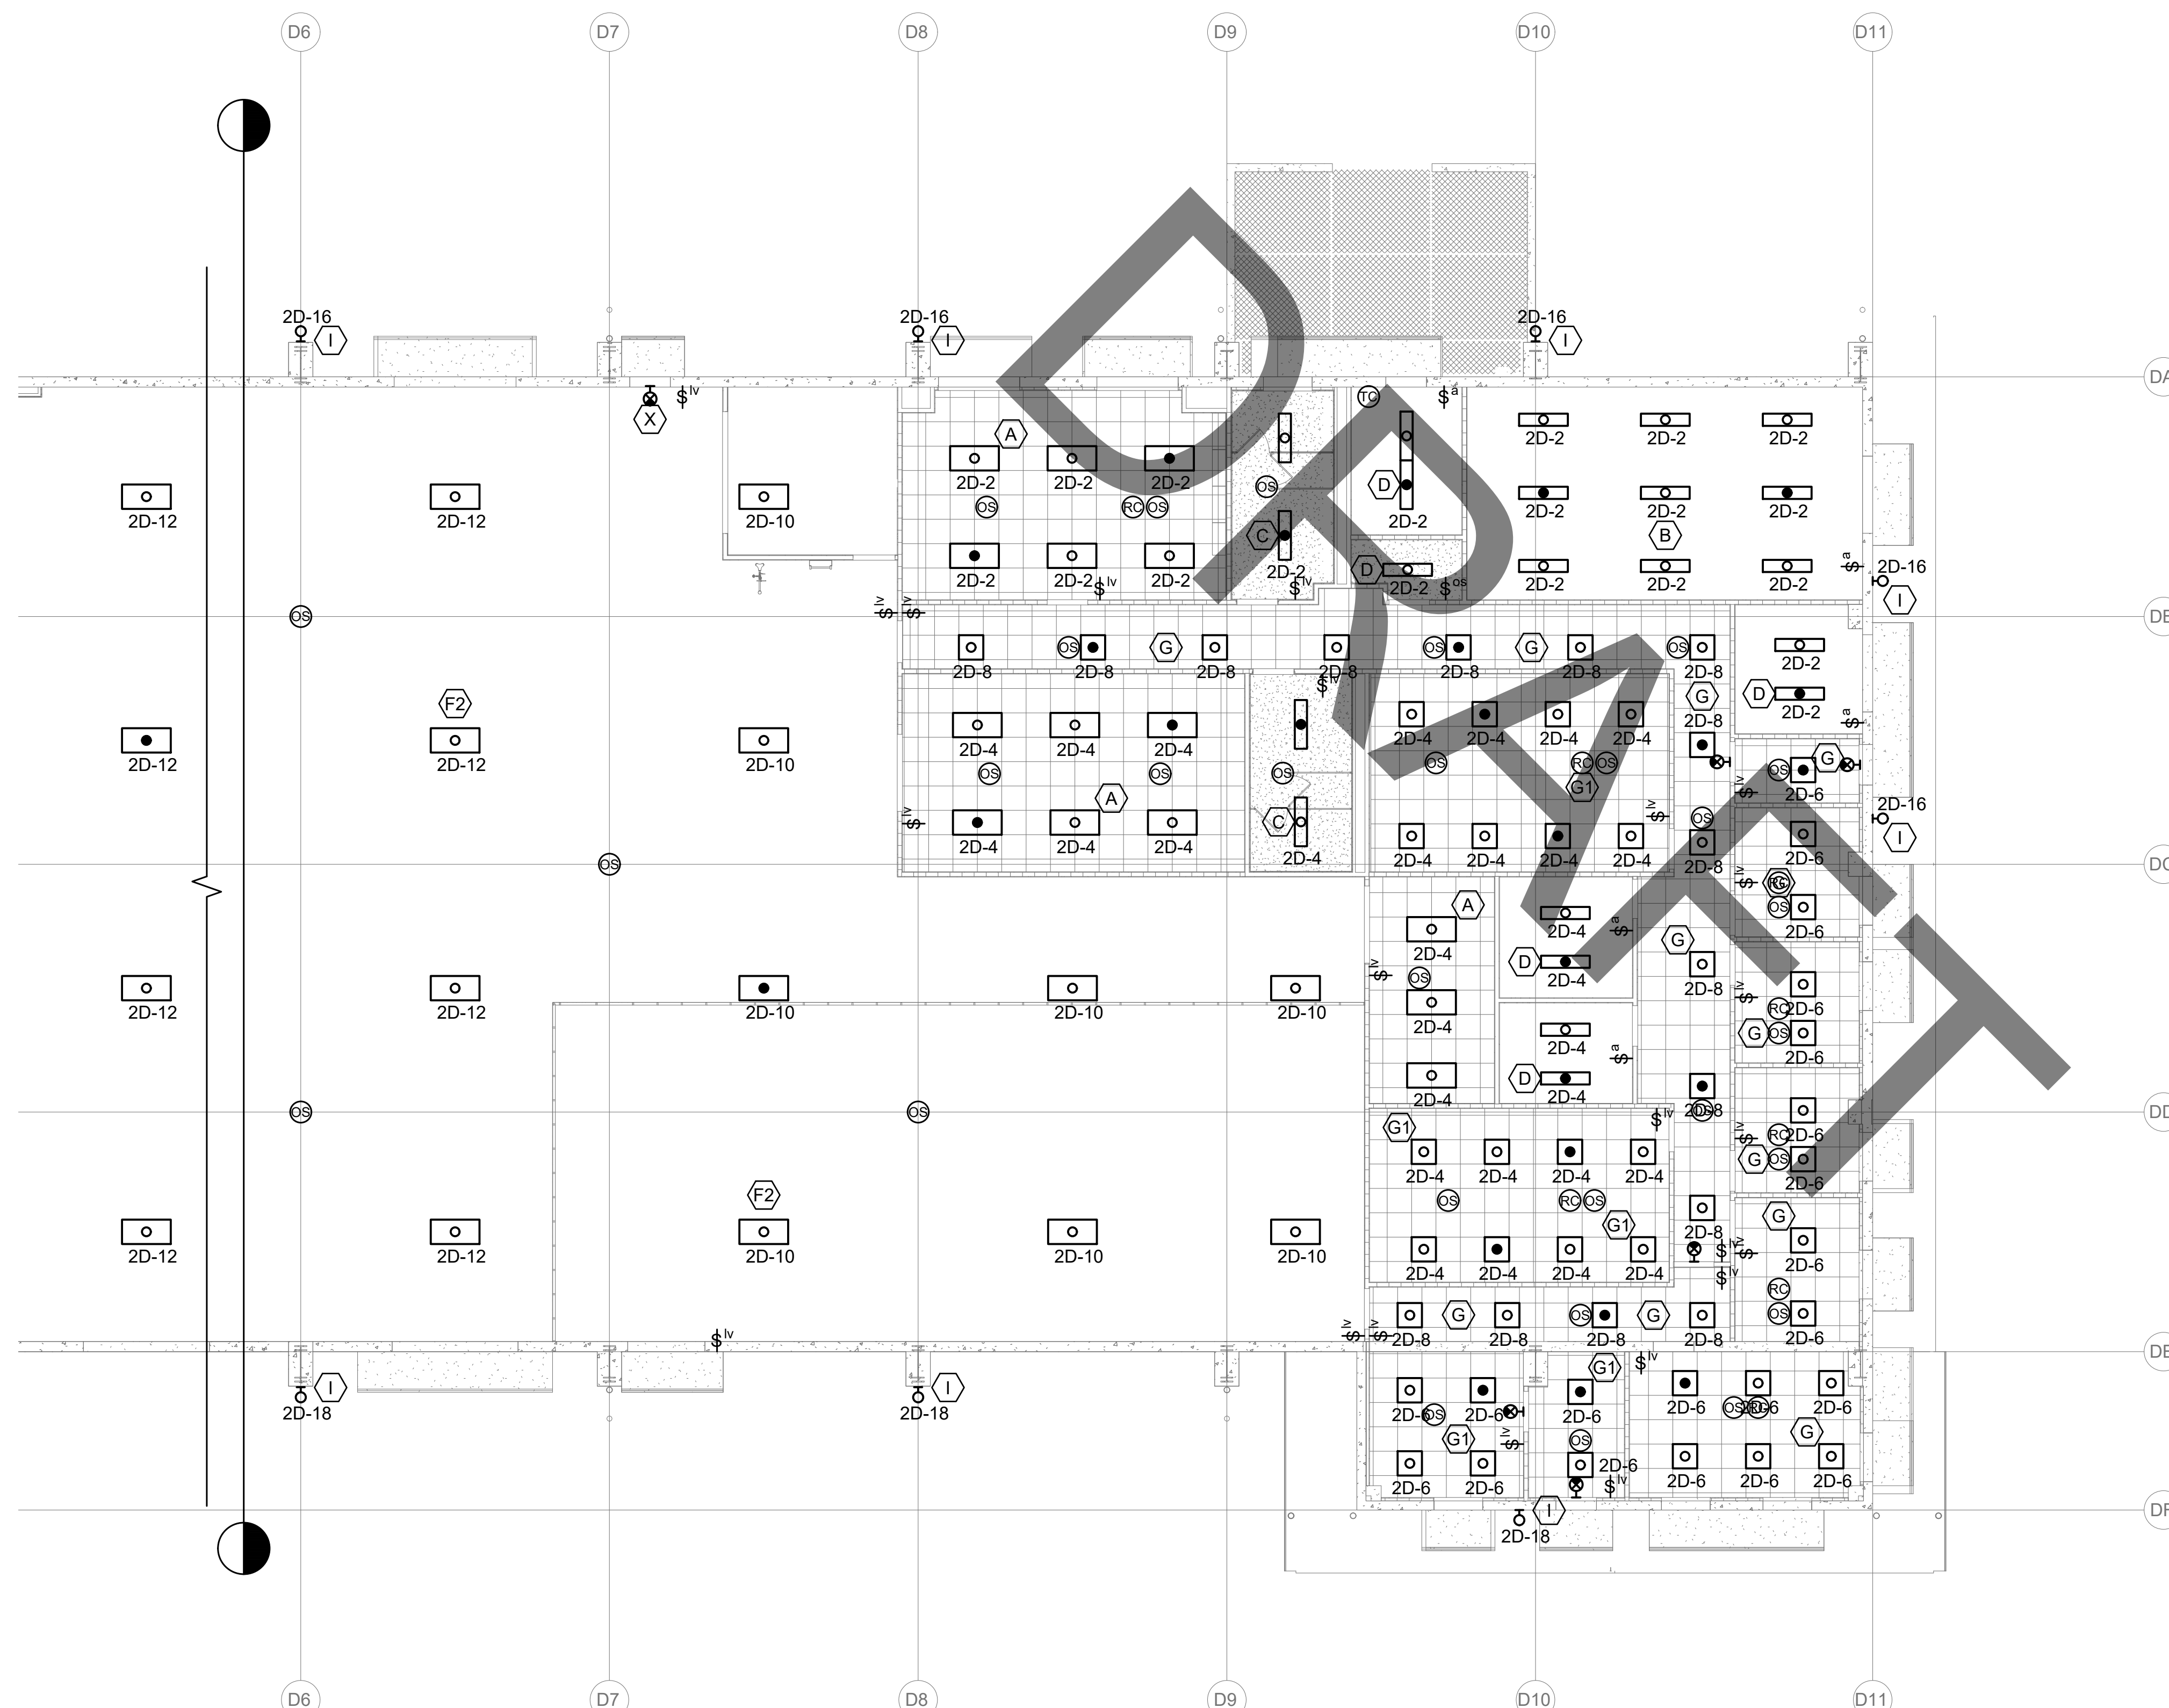

CLIN 0004


KEY PLAN

SSAW
N.T.S.


GRAPHIC SCALE



SCALE: 1 : 100

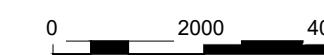


ALL DIMENSIONS AND/OR DIMENSIONS SHOWN IN
CALLOUT/ NOTES ARE IN MILLIMETERS UNLESS
OTHERWISE NOTED.

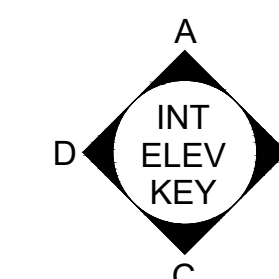

(A1) SSAW - PARTIAL LIGHTING PLAN - ZONE B (CLIN 0004)
1:100

— A — B — C — D — E — F — G — H — I — J — K — L — M — N — O — P

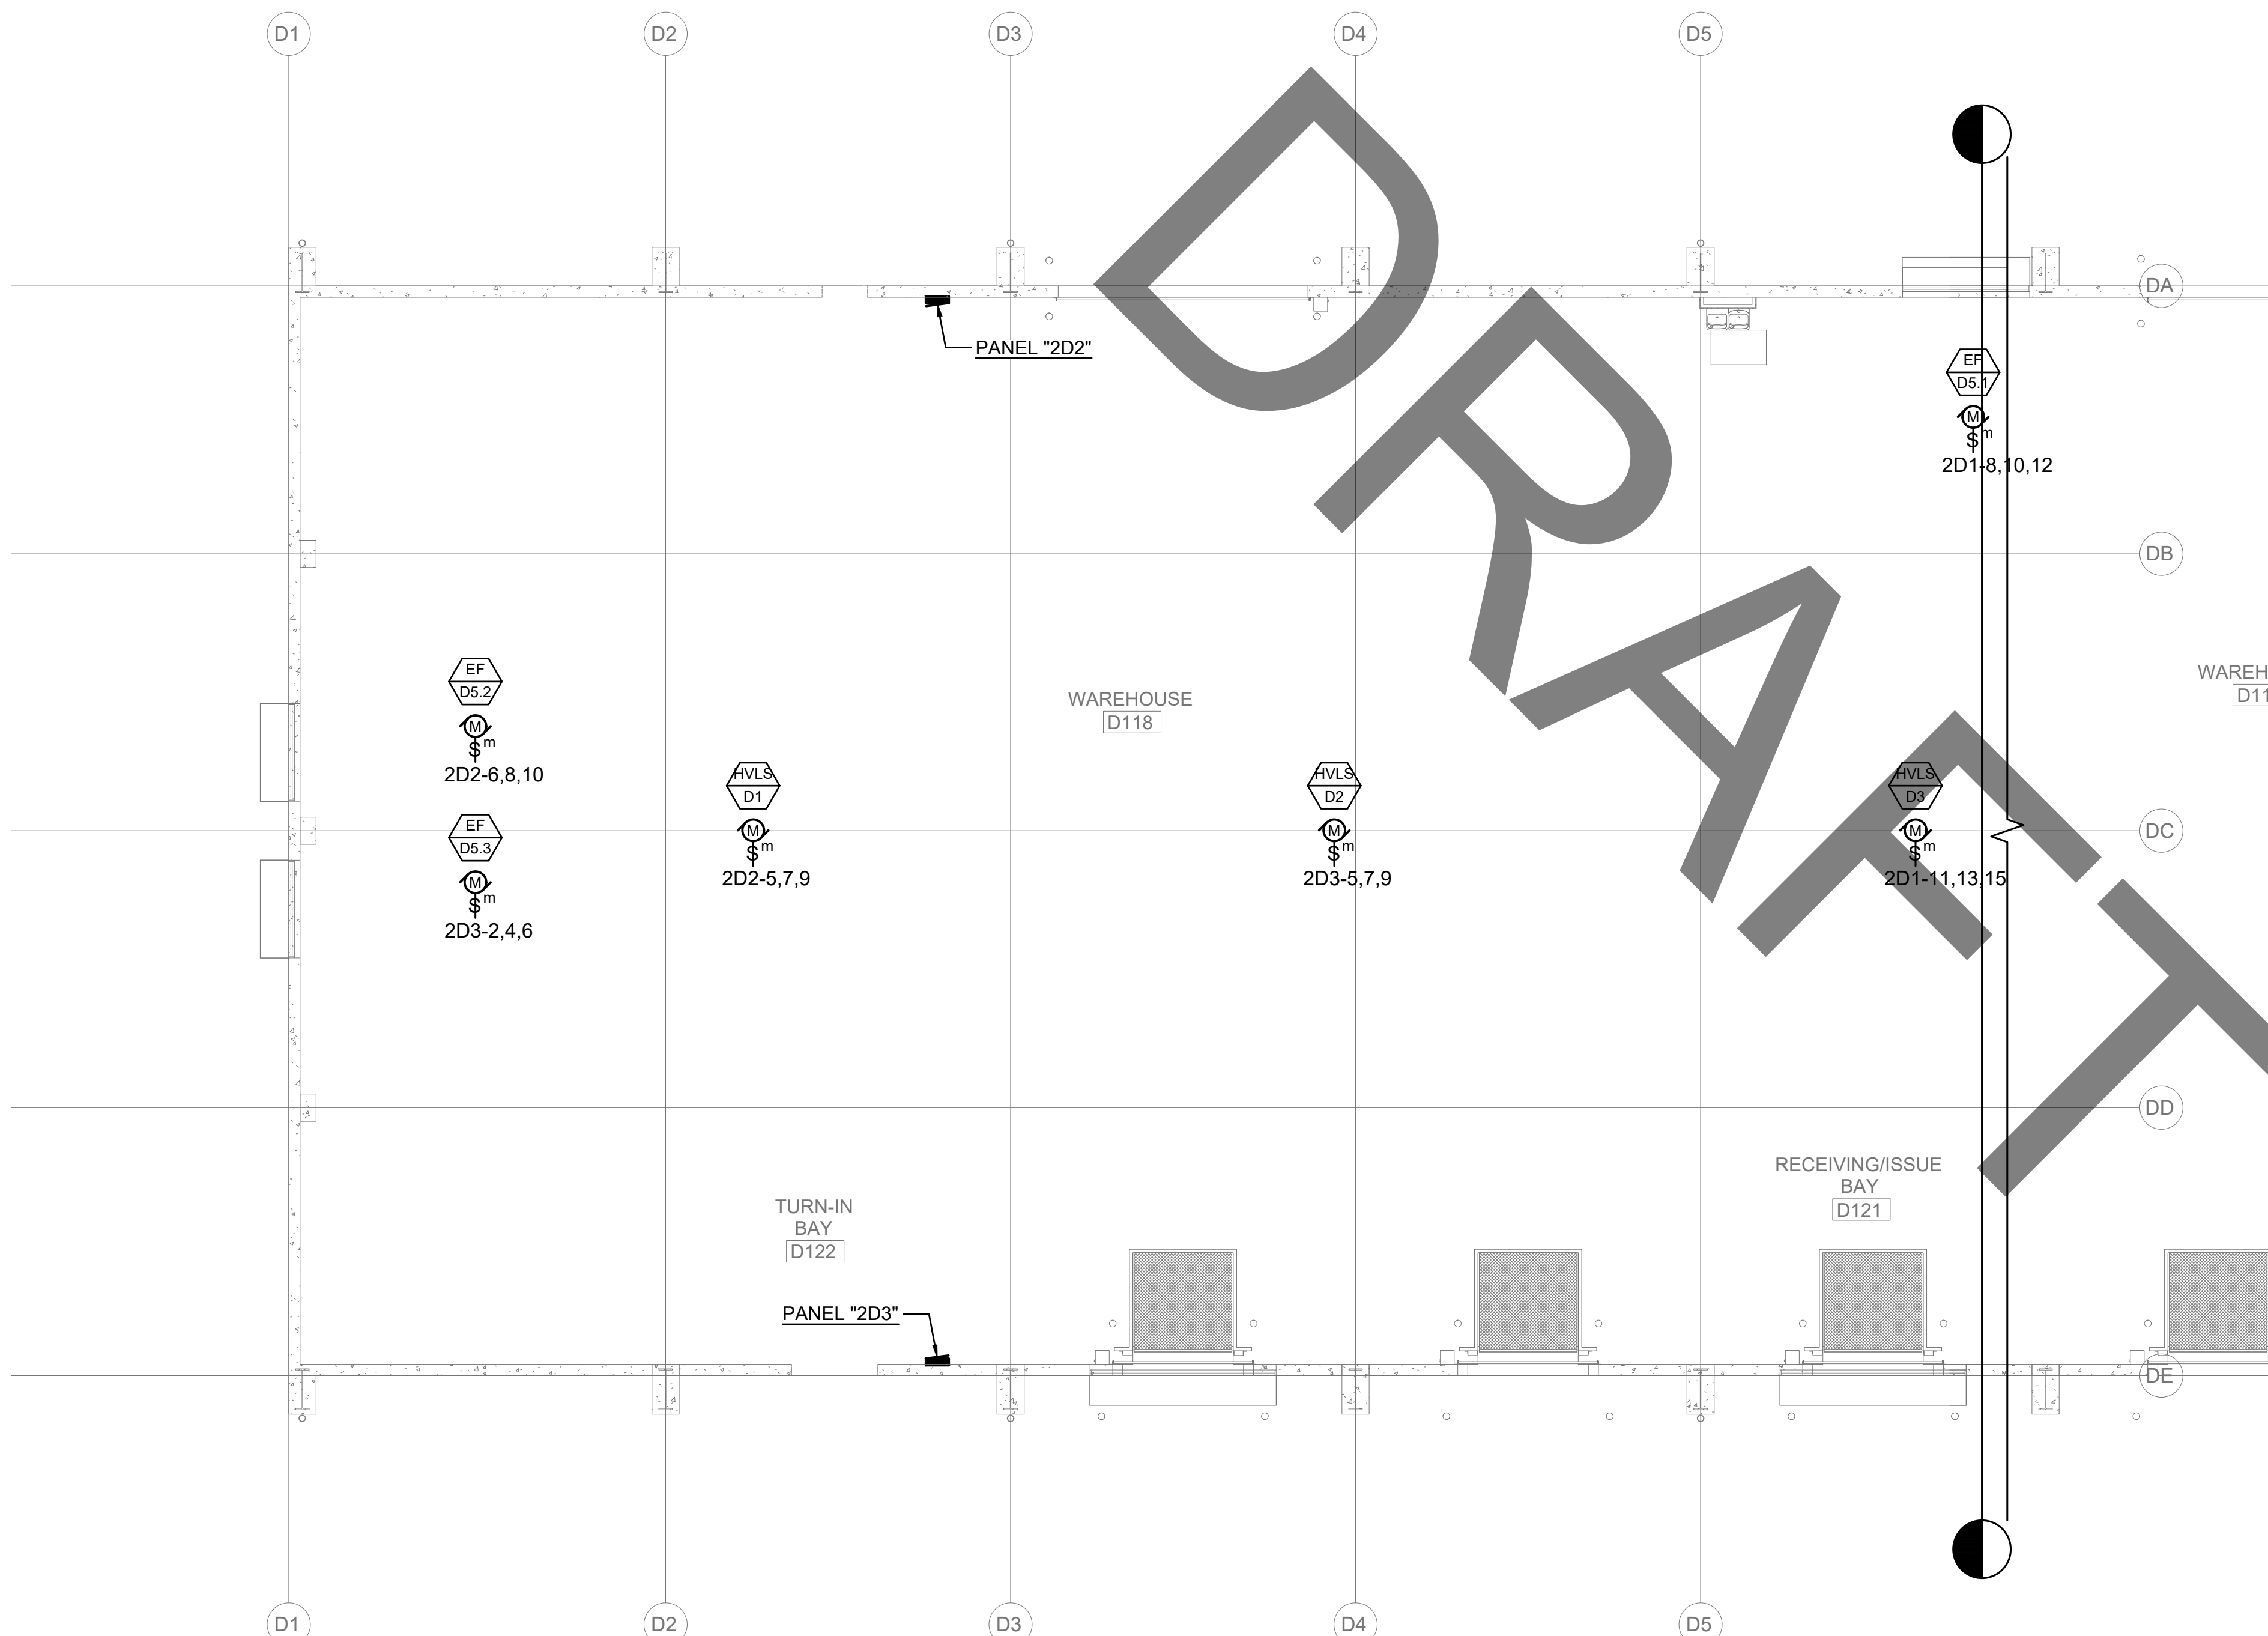

A1 SSWA - PARTIAL MECHANICAL EQUIPMENT POWER PLAN - ZONE A (CLIN 0004)

GENERAL NOTES

1. HVLS SHALL INTERLOCK WITH FIRE ALARM SYSTEM. COORDINATE ALL WORK WITH MECHANICAL AND FIRE PROTECTION.
2. COORDINATE HVLS CONTROLLER LOCATION WITH MECHANICAL.

US Army Corps
of Engineers®[illegible]

DESIGNED BY:	ISSUE DATE:
DRAWN BY:	SOLICITATION NO.:
CHECKED BY:	CONTRACT NO.:
SUBMITTED BY:	SCALE: AS SHOWN
FILE NAME:	SIZE: *

US ARMY CORPS OF ENGINEERS
JAPAN DISTRICT, OKINAWA AREA OFFICE
USED-J UNIT 35132
APO, AP 96374-0132



SSFM INTERNATIONAL, INC.
501 SUMMER STREET, SUITE 620

KADENA AIR BASE, OKINAWA, JAPAN
VEHICLE MAINTENANCE SHOP
FY20 MCA PN77833


SHEET ID

ED131

INTERMEDIATE DESIGN

CLIN 0004



KEY PLAN

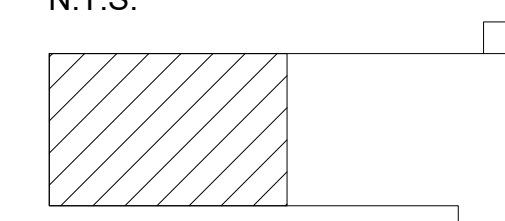SSAW
N.T.S.

GRAPHIC SCALE



SCALE: 1 : 100

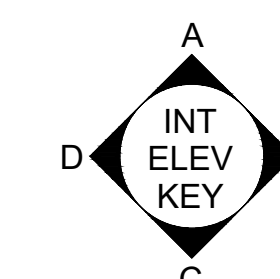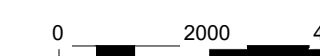


ALL DIMENSIONS AND/OR DIMENSIONS SHOWN IN
CALLOUT/ NOTES ARE IN MILLIMETERS UNLESS
OTHERWISE NOTED.

US Army Corps
of Engineers®

1. HVLS SHALL INTERLOCK WITH FIRE ALARM SYSTEM. COORDINATE ALL WORK WITH MECHANICAL AND FIRE PROTECTION.
2. COORDINATE HVLS CONTROLLER LOCATION WITH MECHANICAL.

[illegible]

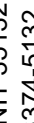
US ARMY CORPS OF ENGINEERS JAPAN DISTRICT, OKINAWA AREA OFFICE USAEJ-1, UNIT 35132 APO, AP 96374-4132		DESIGNED BY: DRAWN BY: CHECKED BY: SUBMITTED BY:	ISSUE DATE: SOLICITATION NO.: CONTRACT NO.: SCALE: AS SHOWN
		S5F1 SUMMER STREET, SUITE 620 551 SUMMER STREET, SUITE 620	FILE NAME: SIZE:

KADENA AIR BASE, OKINAWA, JAPAN
VEHICLE MAINTENANCE SHOP
FY20 MCA PN77833

SHEET ID

ED132

INTERMEDIATE DESIGN

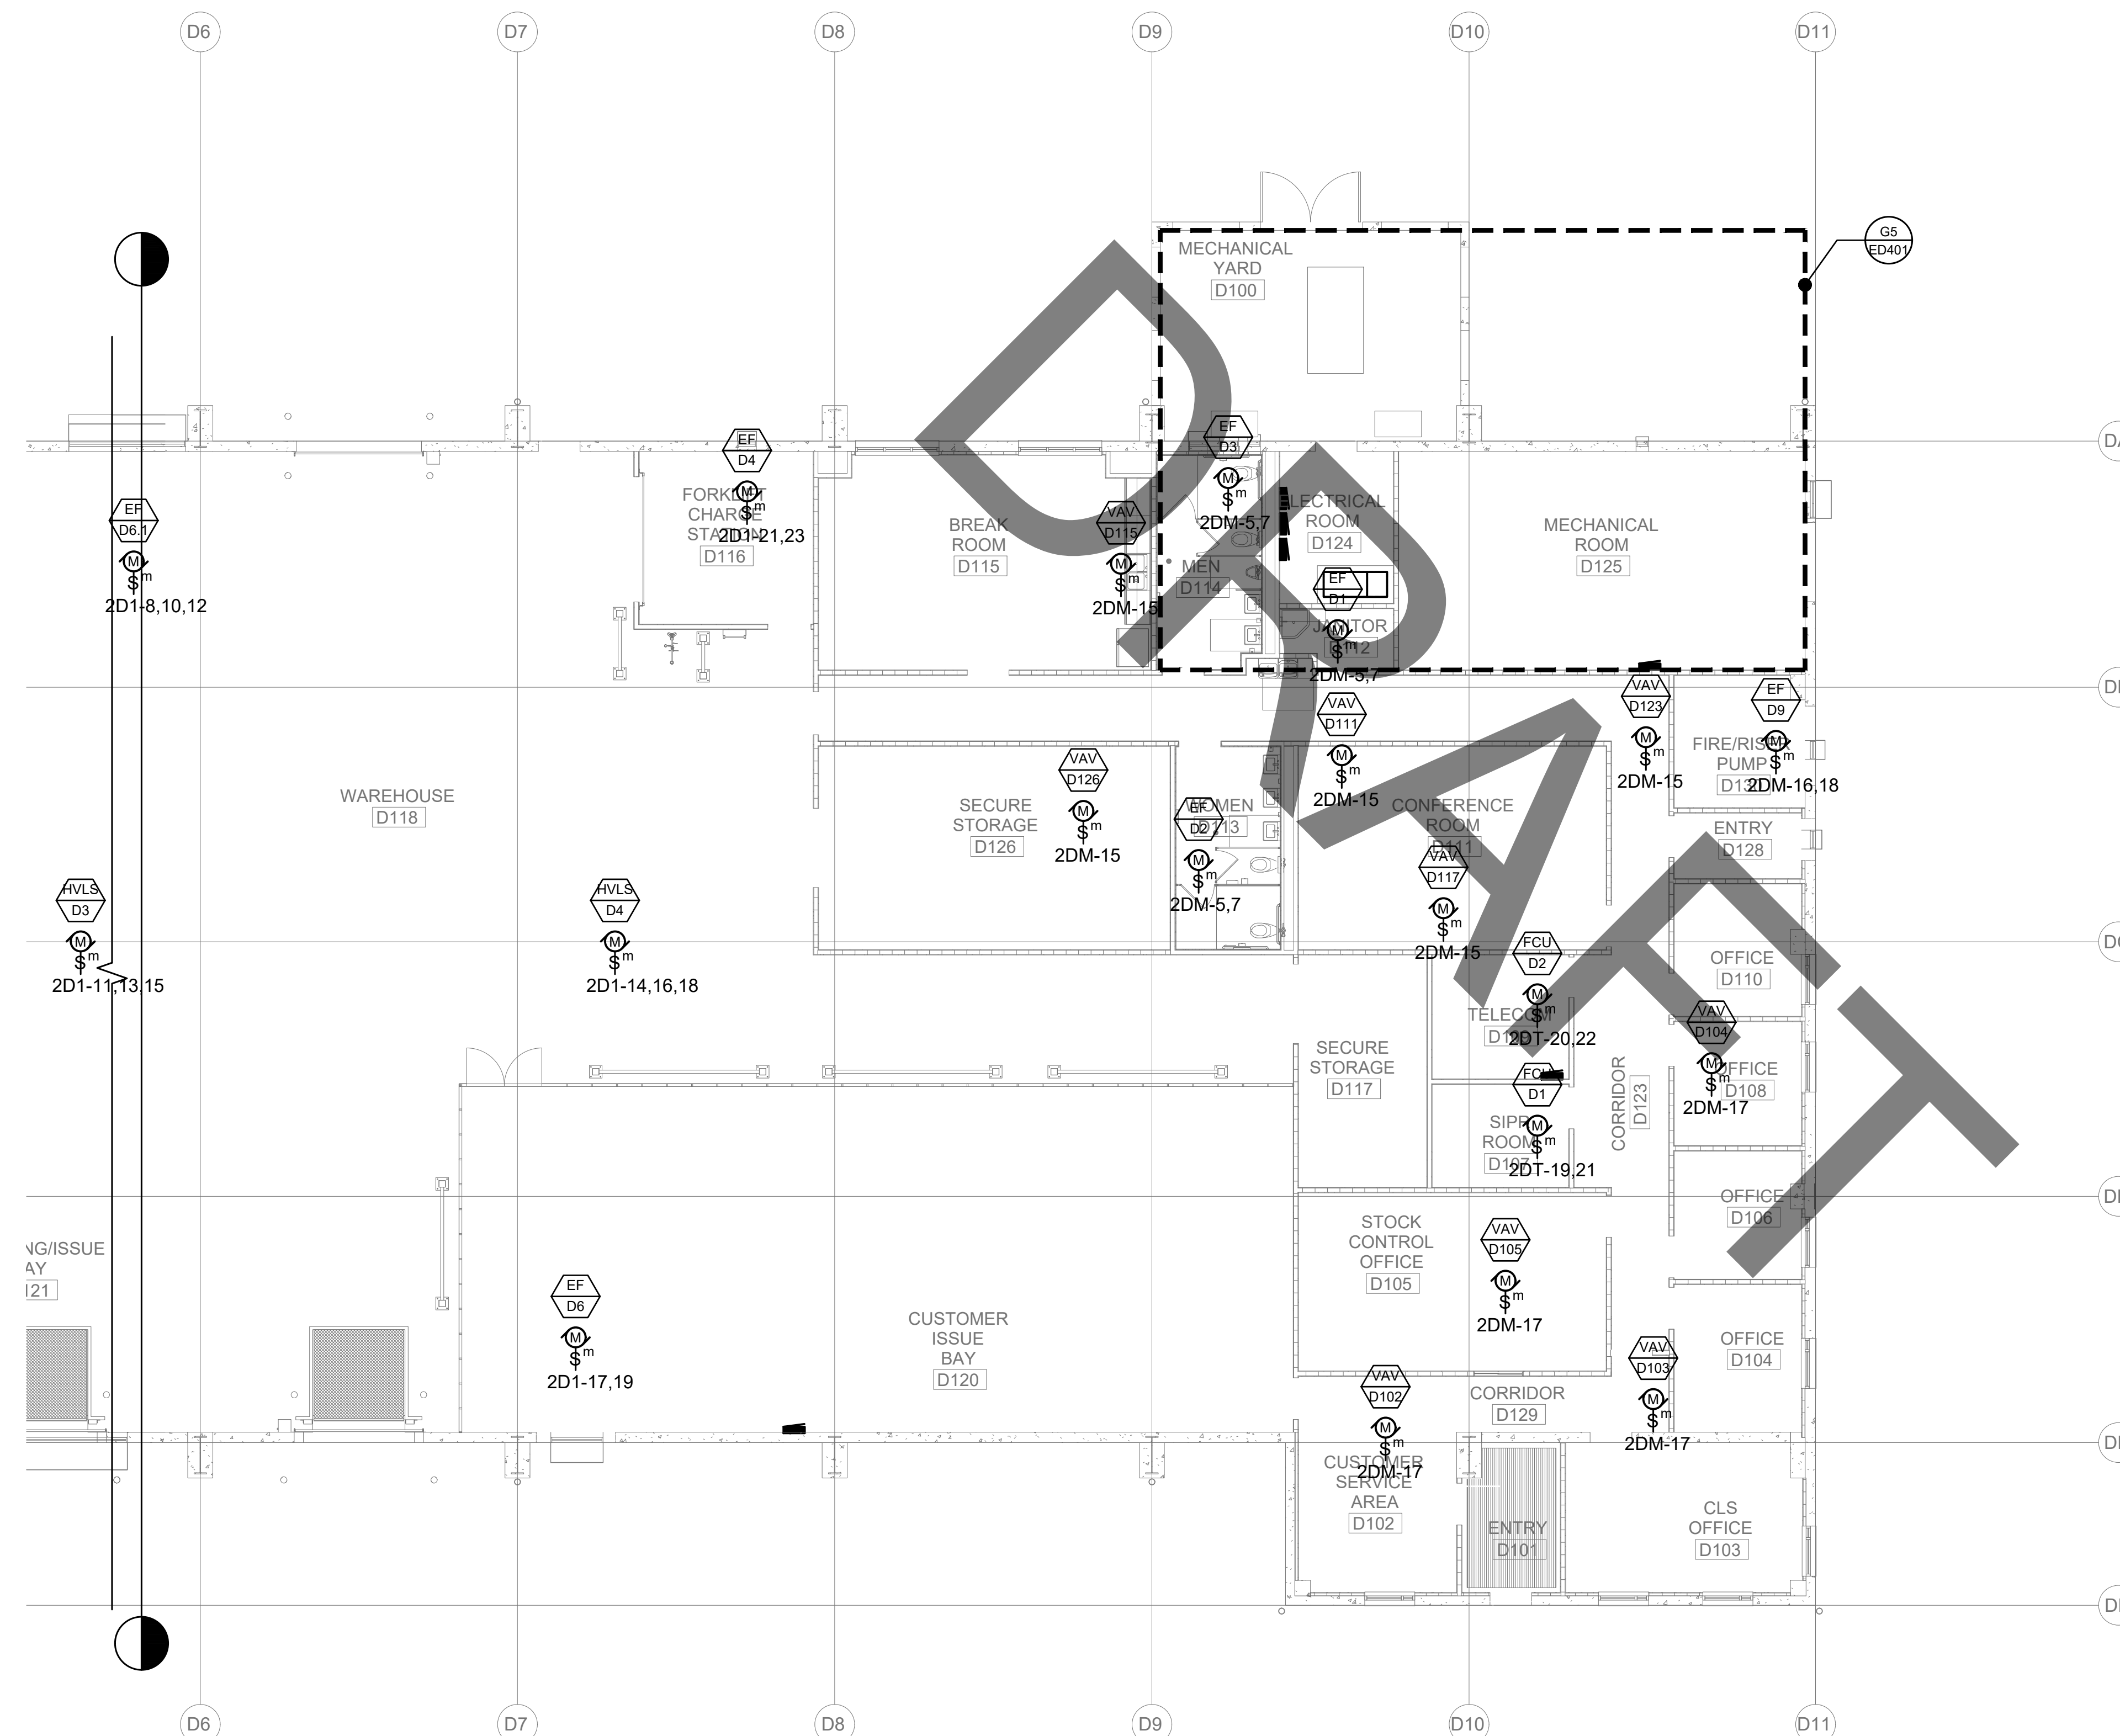


CLIN 0004


KEY PLAN

SSAW
N.T.S.

GRAPHIC SCALE

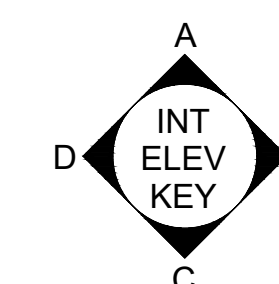

PLAN
NORTH

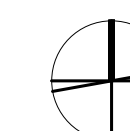


SCALE: 1 : 100

ALL DIMENSIONS AND/OR DIMENSIONS SHOWN IN
CALLOUT/ NOTES ARE IN MILLIMETERS UNLESS
OTHERWISE NOTED.


SSAW - PARTIAL MECHANICAL EQUIPMENT POWER PLAN - ZONE B (CLIN 0004)

1:100

A — B — C — D — E — F — G — H — I — J — K — L — M — N — O — P —

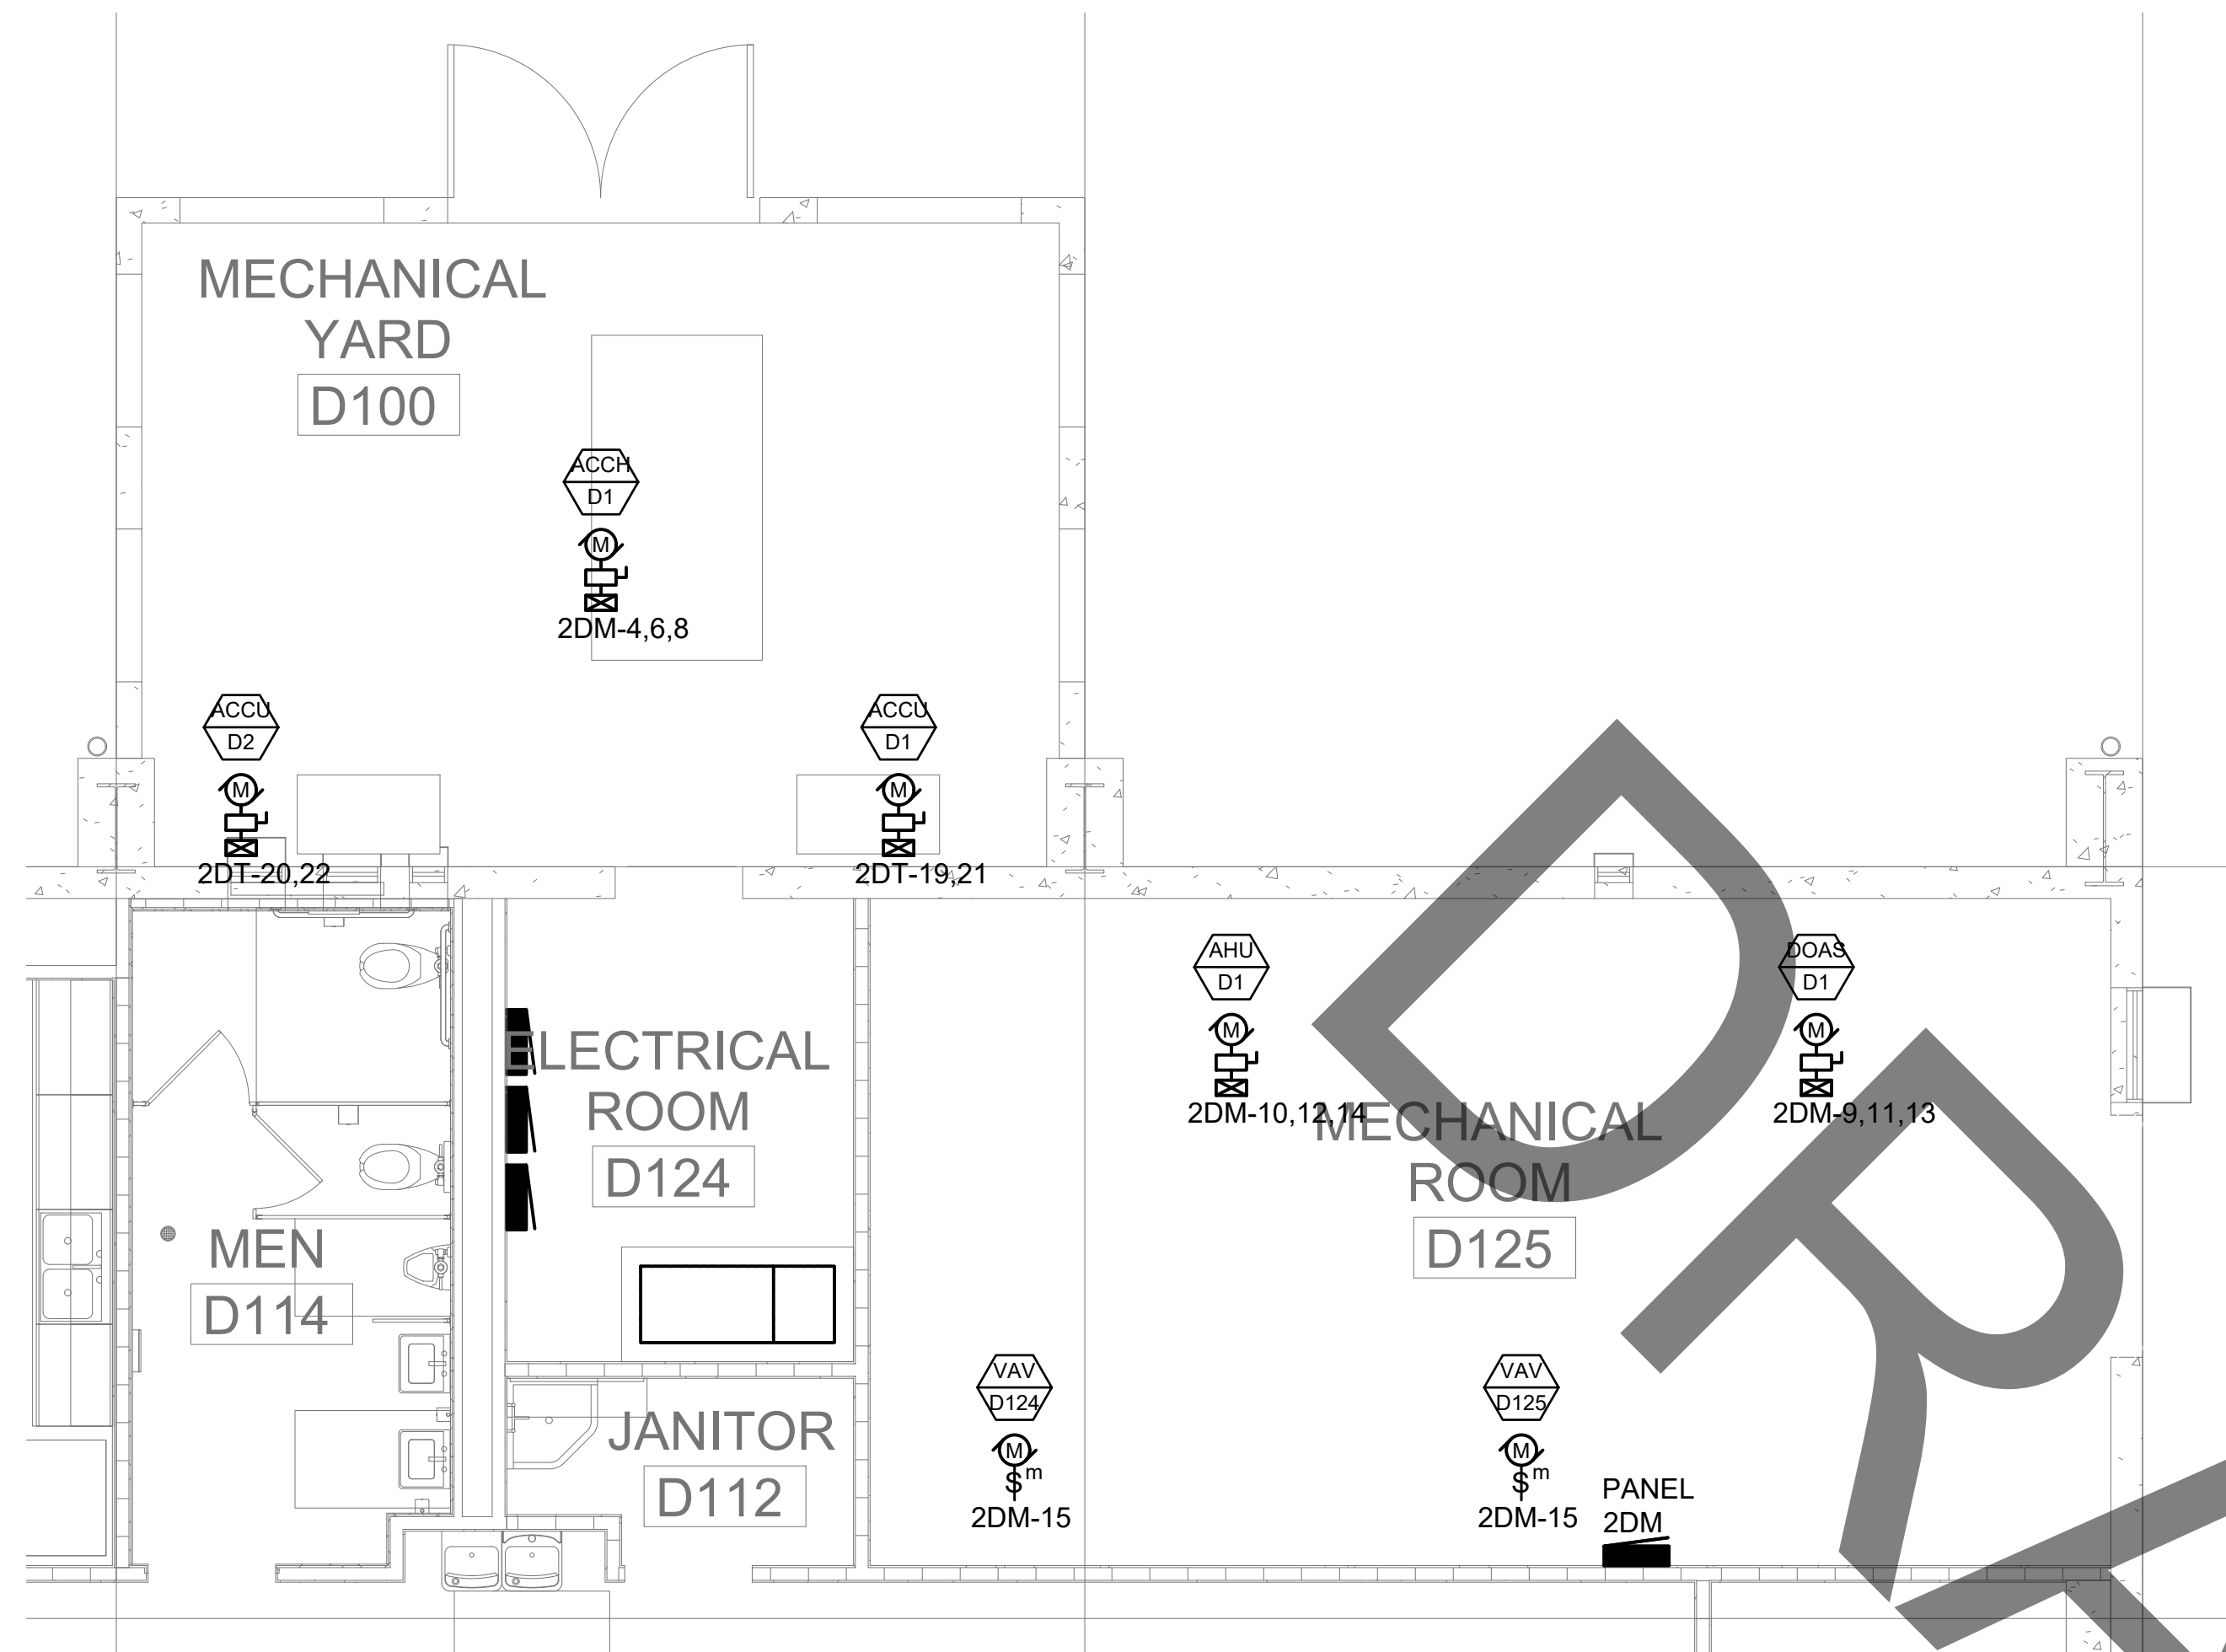

G5 **SSAW - ENLARGED MECH ROOM & MECH YARD (CLIN 0004)**
1:50

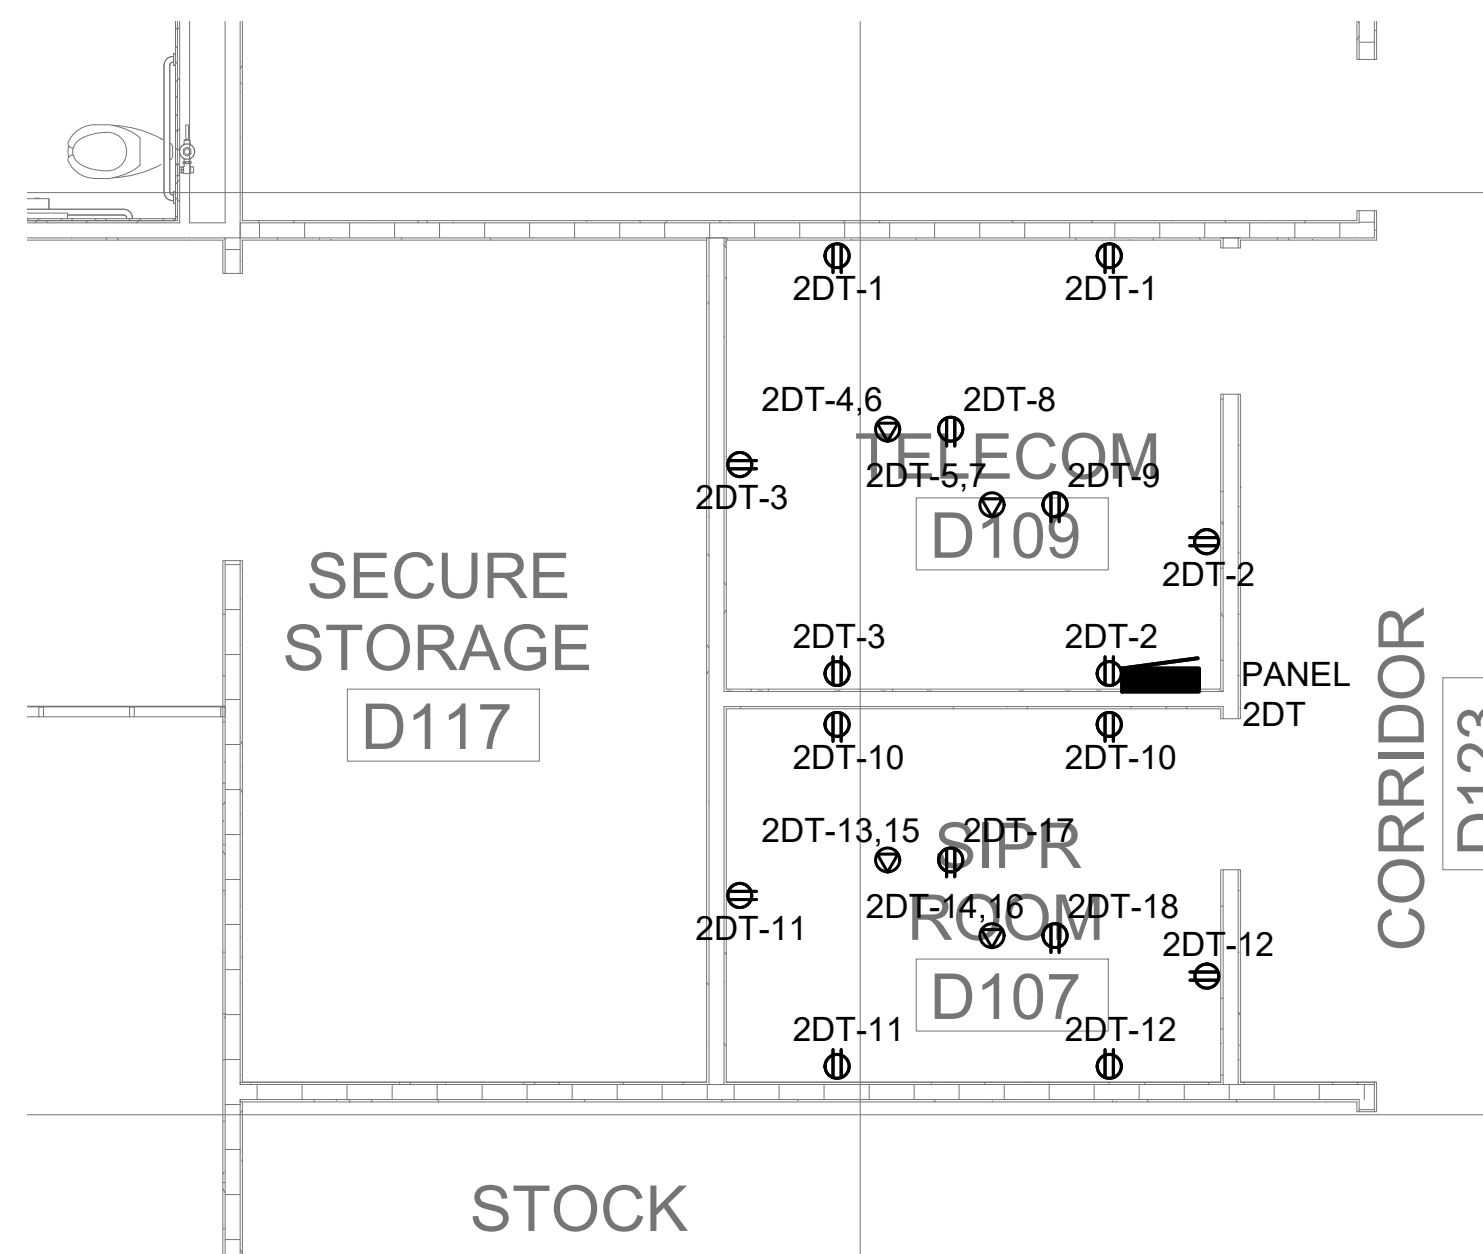

(A5) SSAW - ENLARGED COMM & SIPR ROOM PLAN (CLIN 0004)
1:50

GENERAL NOTES



US Army Corps
of Engineers®

[illegible]

JAPAN DISTRICT, OKINAWA AREA OFFICE		SOLICITATION NO.:	
USAEJ-1 Unit 35132		DRAWN BY:	
APO, AP 96374-5132		CHECKED BY:	
		CONTRACT NO.:	
SSFM INTERNATIONAL, INC.		SUBMITTED BY:	
501 KALANANUE AVE #20		AS SHOWN	
HONOLULU, HAWAII 96817		SIZE:	FILE NAME:
		ISO A1	

SSAW - ENLARGED PLANS (CLIN 0004)

SHEET ID

ED401

INTERMEDIATE DESIGN

CLIN 0004


GRAPHIC SCALE



SCALE: 1 : 50



ALL DIMENSIONS AND/OR DIMENSIONS SHOWN IN
CALLOUT/ NOTES ARE IN MILLIMETERS UNLESS
OTHERWISE NOTED.

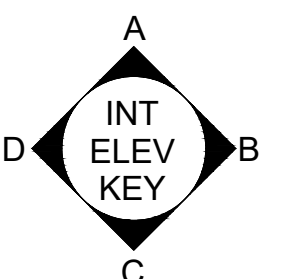

[illegible]


JAPAN DISTRICT, OKINAWA AREA OFFICE USAED-J, UNIT 35132 APO, AF 96374-5132		SSFM INTERNATIONAL, INC. 501 SUMNER STREET, SUITE 620
	DRAWN BY:	SOLICITATION NO.:
	CHECKED BY:	CONTRACT NO.:
	SUBMITTED BY:	SCALE: AS SHOWN
SIZE:	FILE NAME:	

MADEIRA AIR BASE, OKINAWA, JAPAN
VEHICLE MAINTENANCE SHOP
FY20 MCA PN77833

SHEET ID

ED601

INTERMEDIATE DESIGN

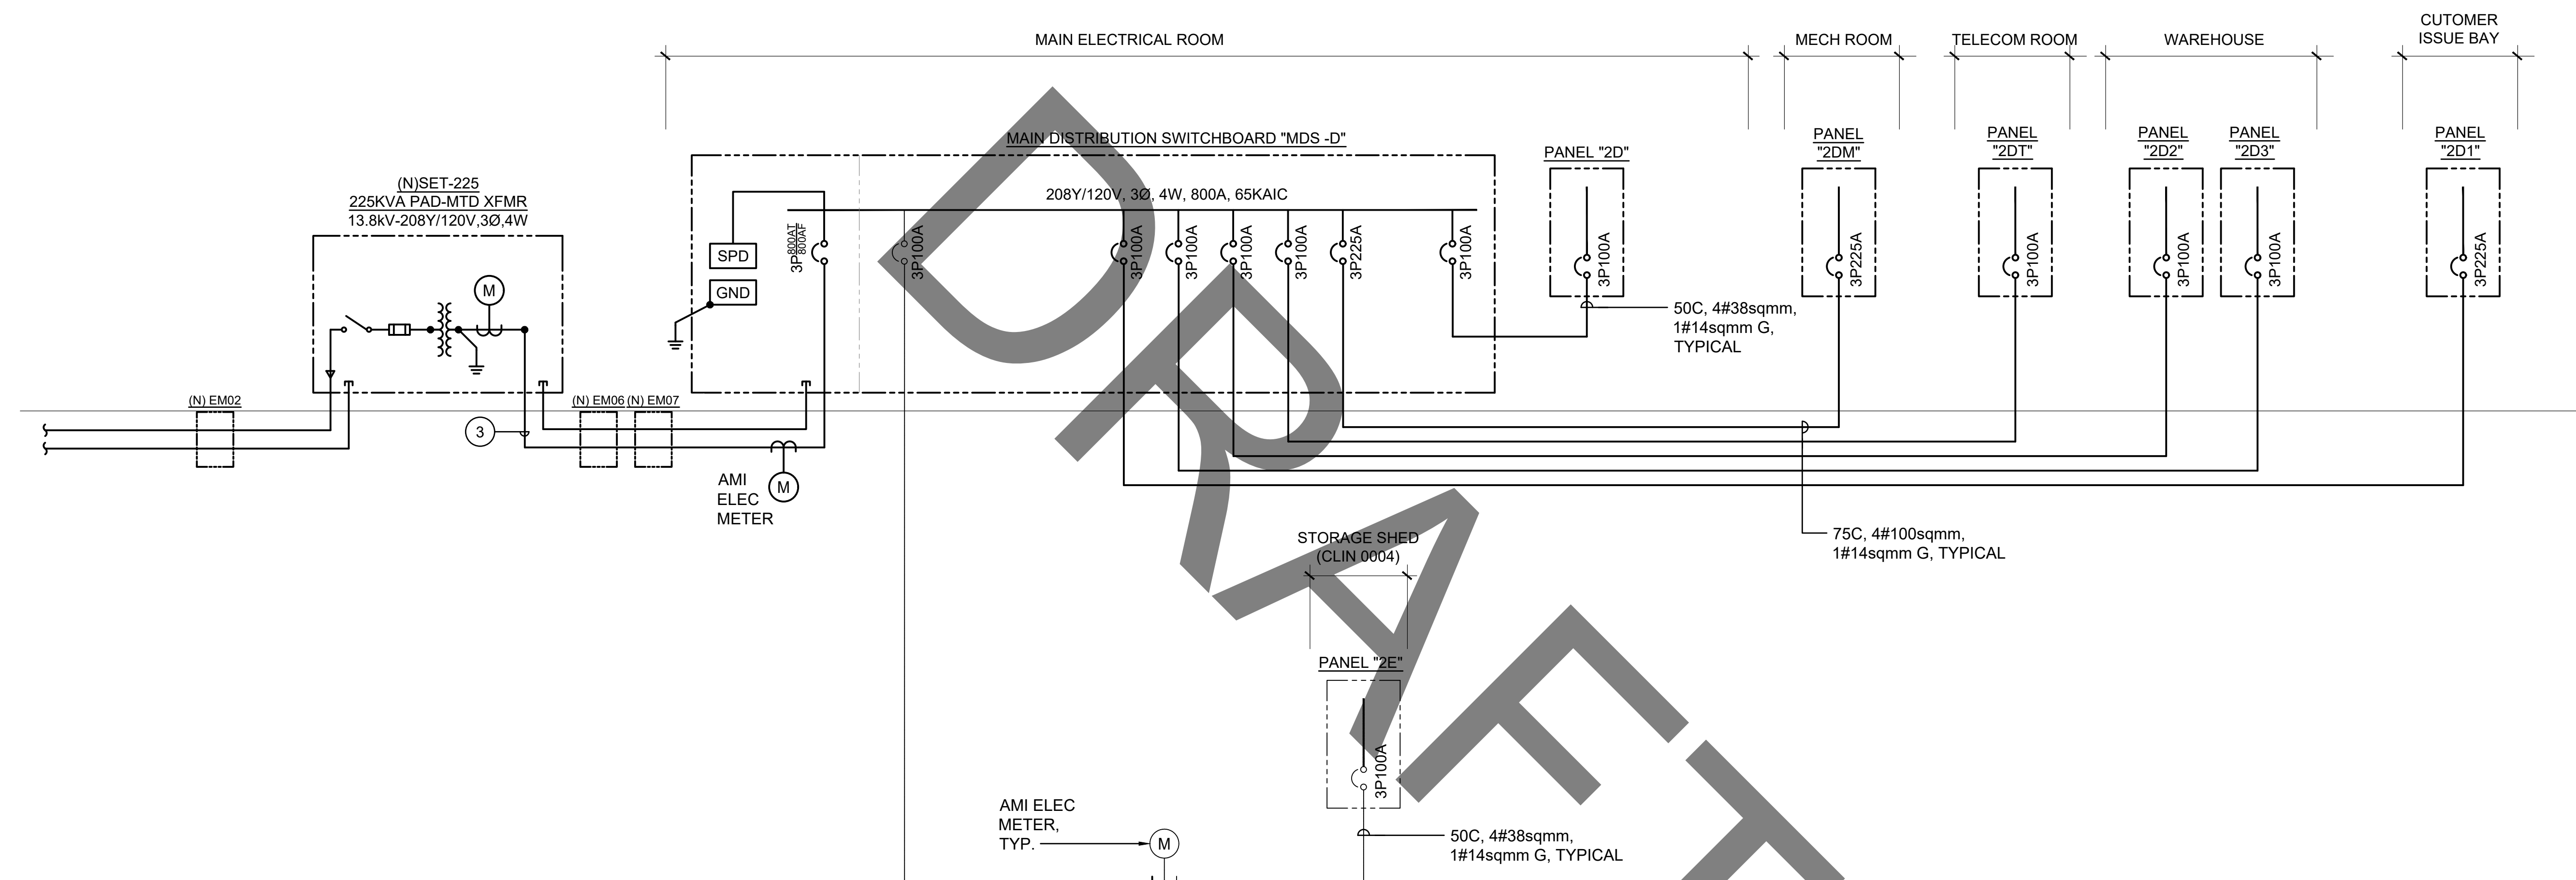

NOTES:

1. REFER TO SITE PLANS FOR PHASING AND WORK INVOLVED IN CLIN 0001, CLIN 0002, CLIN 0003, CLIN 0004.
2. REFER TO SITE PLANS FOR FEEDER INFO AND SITE DISTRIBUTION.


A1 SSAW - ONE-LINE DIAGRAM (CLIN 0004)
NONE

CLIN 0004

[illegible][illegible]

INTERMEDIATE DESIGN

— A — B — C — D — E — F — G — H — I — J — K — L — M — N — O — P

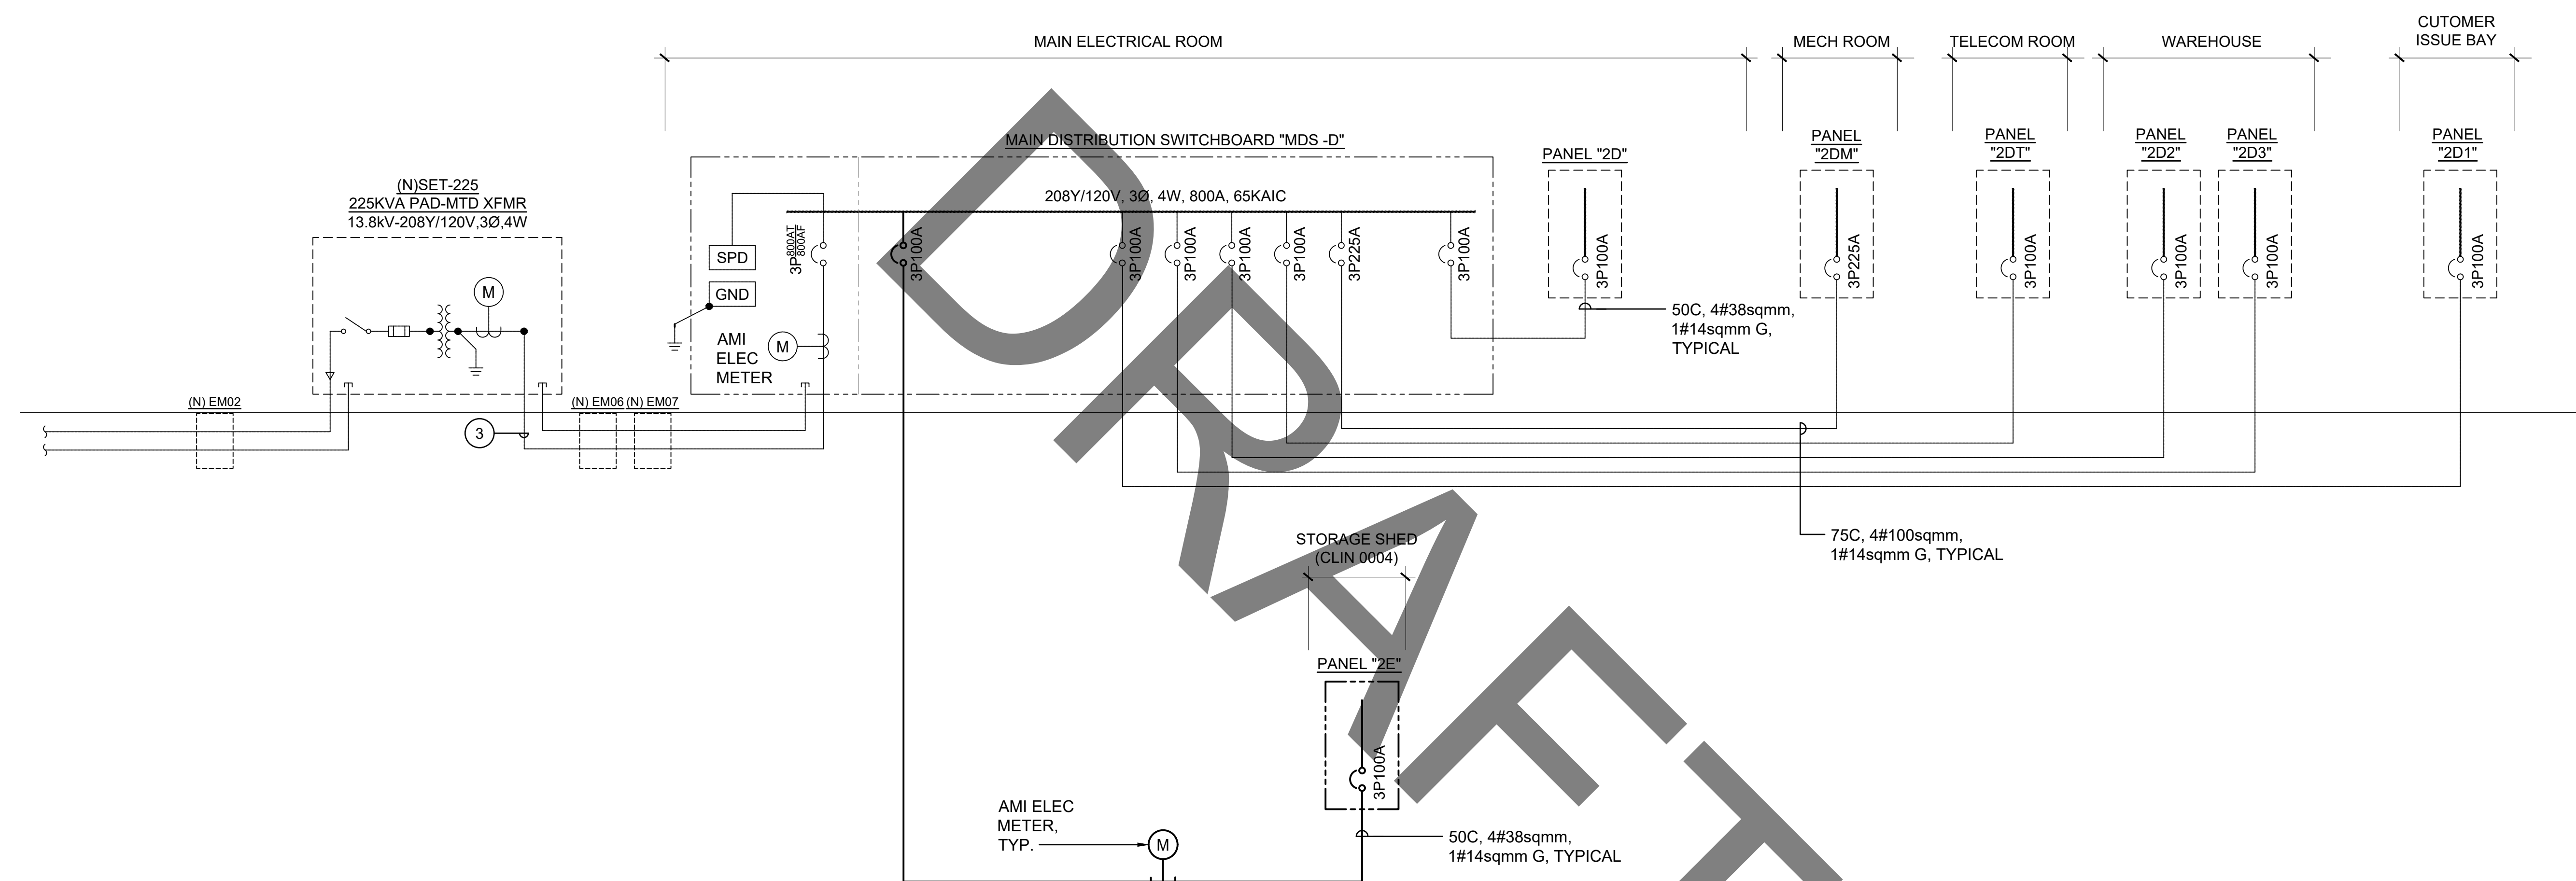

NOTES:

1. REFER TO SITE PLANS FOR PHASING AND WORK INVOLVED IN CLIN 0001, CLIN 0002, CLIN 0003, CLIN 0004.
2. REFER TO SITE PLANS FOR FEEDER INFO AND SITE DISTRIBUTION.

A1 SS - ONE-LINE DIAGRAM (CLIN 0004)
NONE

CLIN 0004

US Army Corps
of Engineers®[illegible]

US ARMY CORPS OF ENGINEERS JAPAN DISTRICT, OKINAWA AREA OFFICE USAEJ-1, UNIT 35132 APO, AP 96374-5132	DESIGNED BY:	ISSUE DATE:
	DRAWN BY:	SOLICITATION NO.:
 SFSM INTERNATIONAL, INC. 501 SUMMER STREET, SUITE 620	CHECKED BY:	CONTRACT NO.:
	SUBMITTED BY:	SCALE: AS SHOWN
	SIZE:	FILE NAME:

KADENA AIR BASE, OKINAWA, JAPAN
VEHICLE MAINTENANCE SHOP
FY20 MCA PN77833

SHEET ID

EE601

INTERMEDIATE DESIGN

[illegible]


JAPAN DISTRICT, OKINAWA AREA OFFICE USAED-J, UNIT 35132 APO, AP 96374-5132	DRAWN BY: CHECKED BY: SUBMITTED BY: SCALE: AS SHOWN	SOLICITATION NO.: CONTRACT NO.:
 SSFM International SSFM INTERNATIONAL, INC 501 SUMNER STREET, SUITE 620		
SIZE: FILE NAME:		

MAZDA/FAIR DUEL ON/MAZDA - JAPAN
VEHICLE MAINTENANCE SHOP
F Y20 MCA PN77833

SHEET ID

EF601


INTERMEDIATE DESIGN

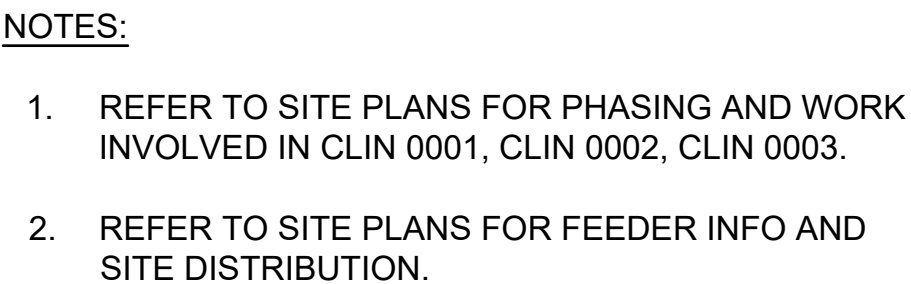


A1 FP - ONE-LINE DIAGRAM (CLIN 0001)
NONE

CLIN 0001


A — B — C — D — E — F — G — H — I — J — K — L — M — N — O — P

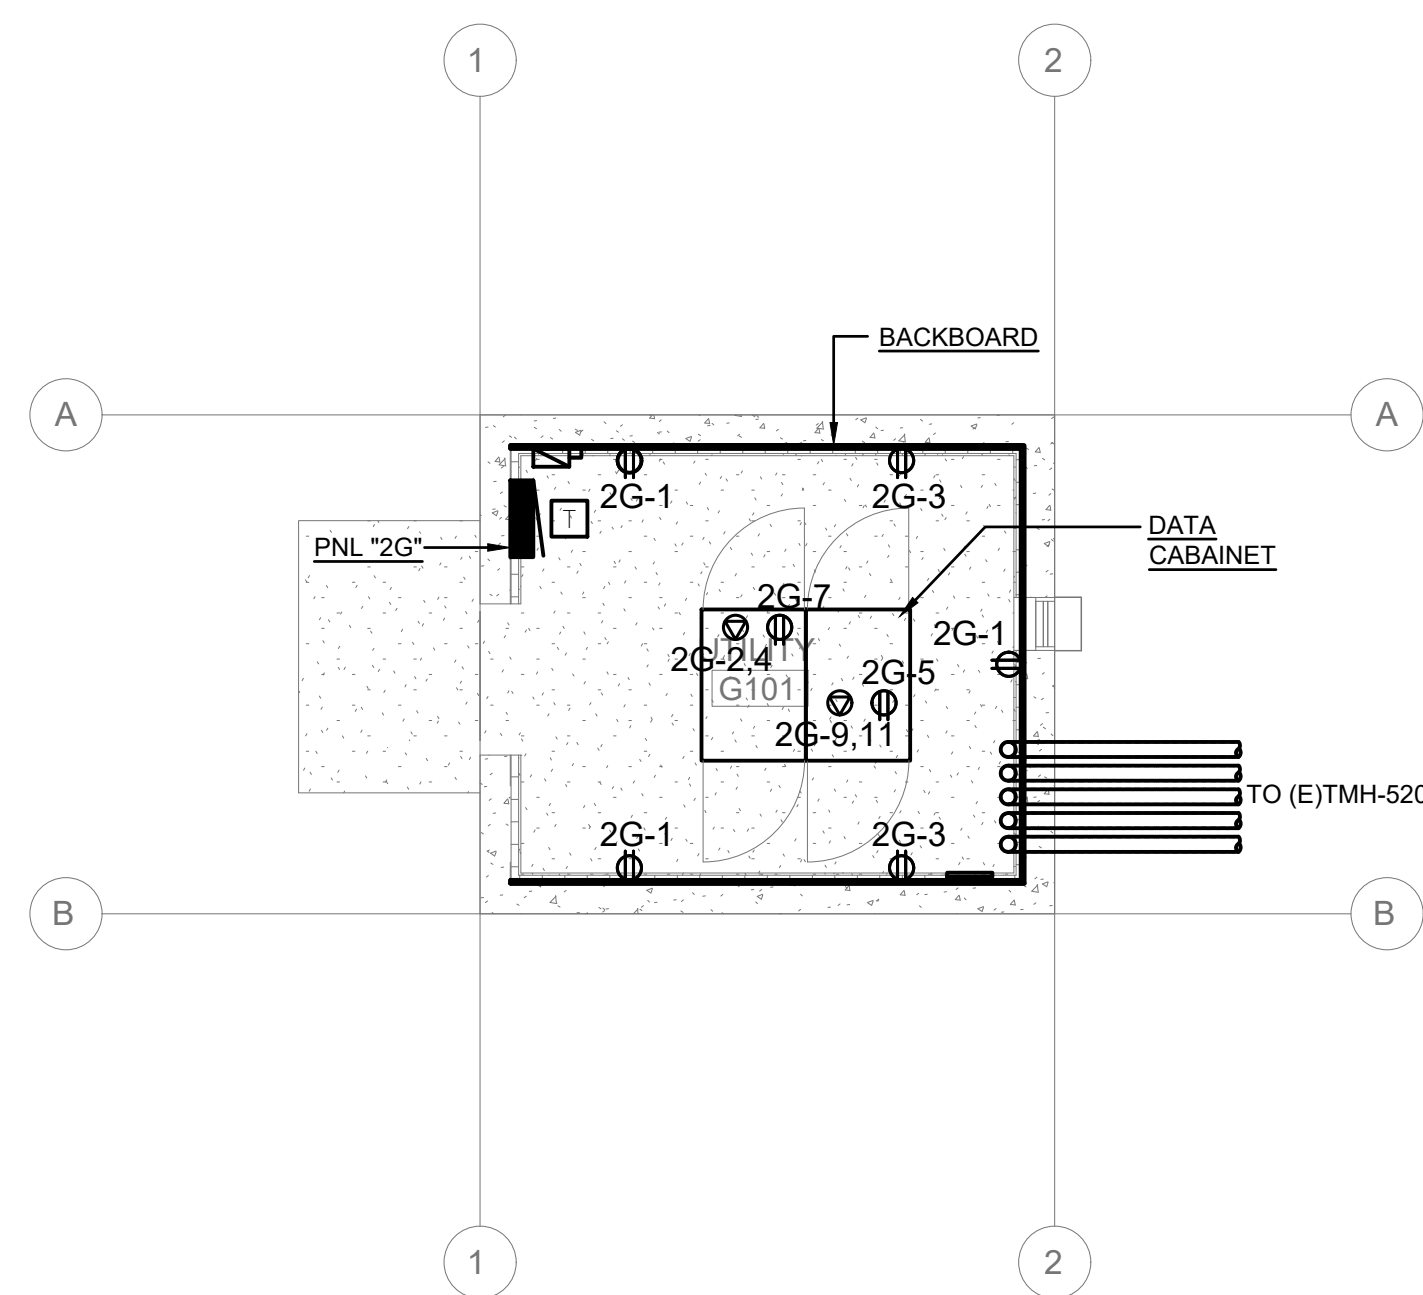


12 CH - POWER PLAN (CLIN 0001)

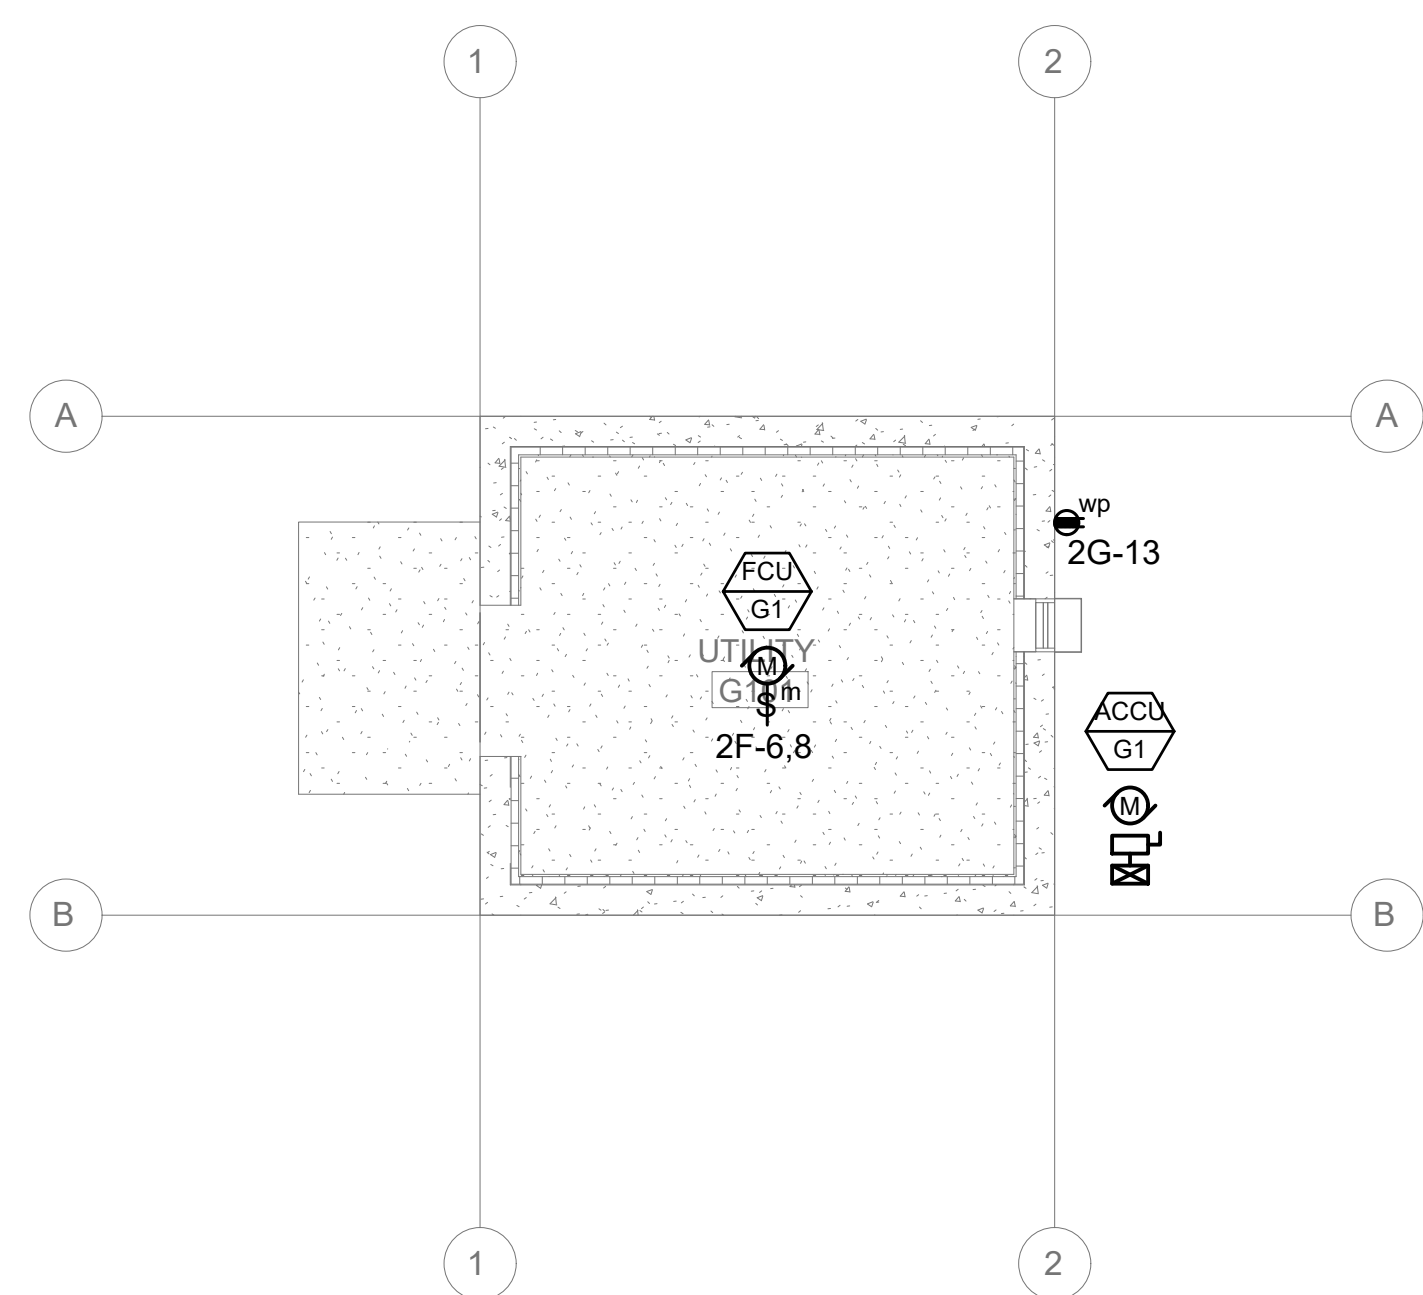

(B2) CH - MECHANICAL PLAN (CLIN 0001)

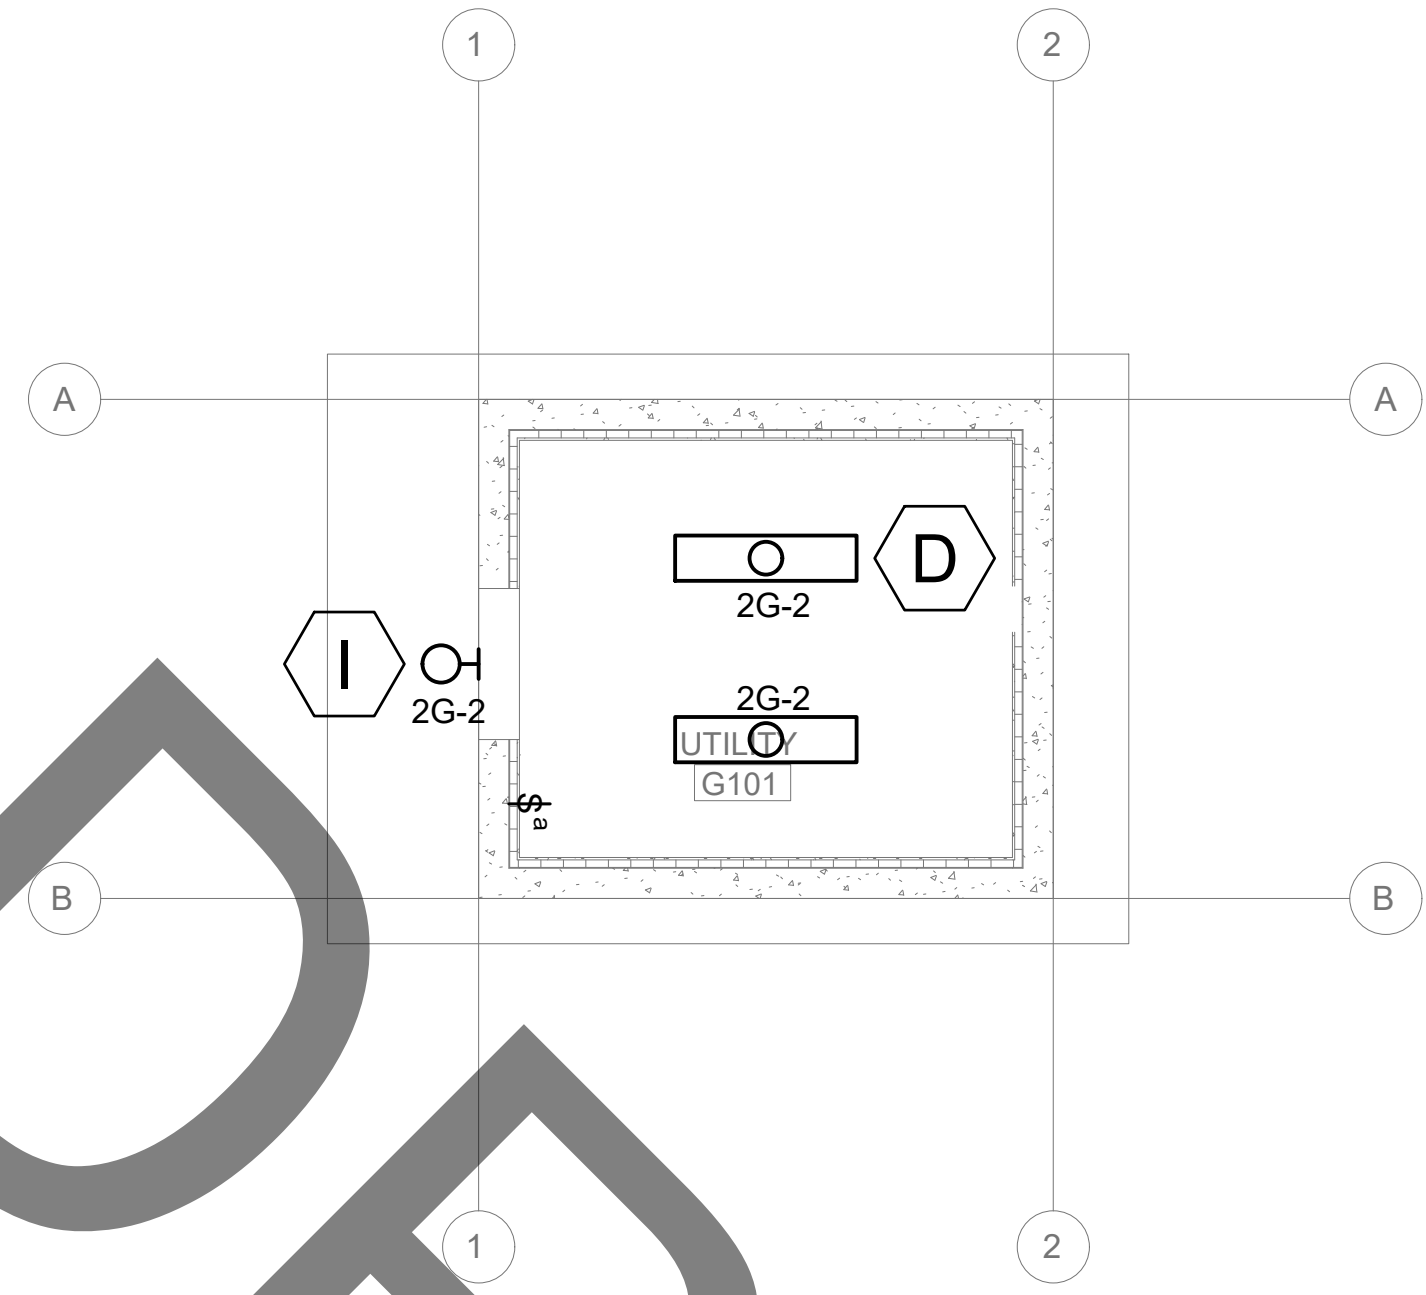


19 CH - LIGHTING PLAN (CLIN 0001)

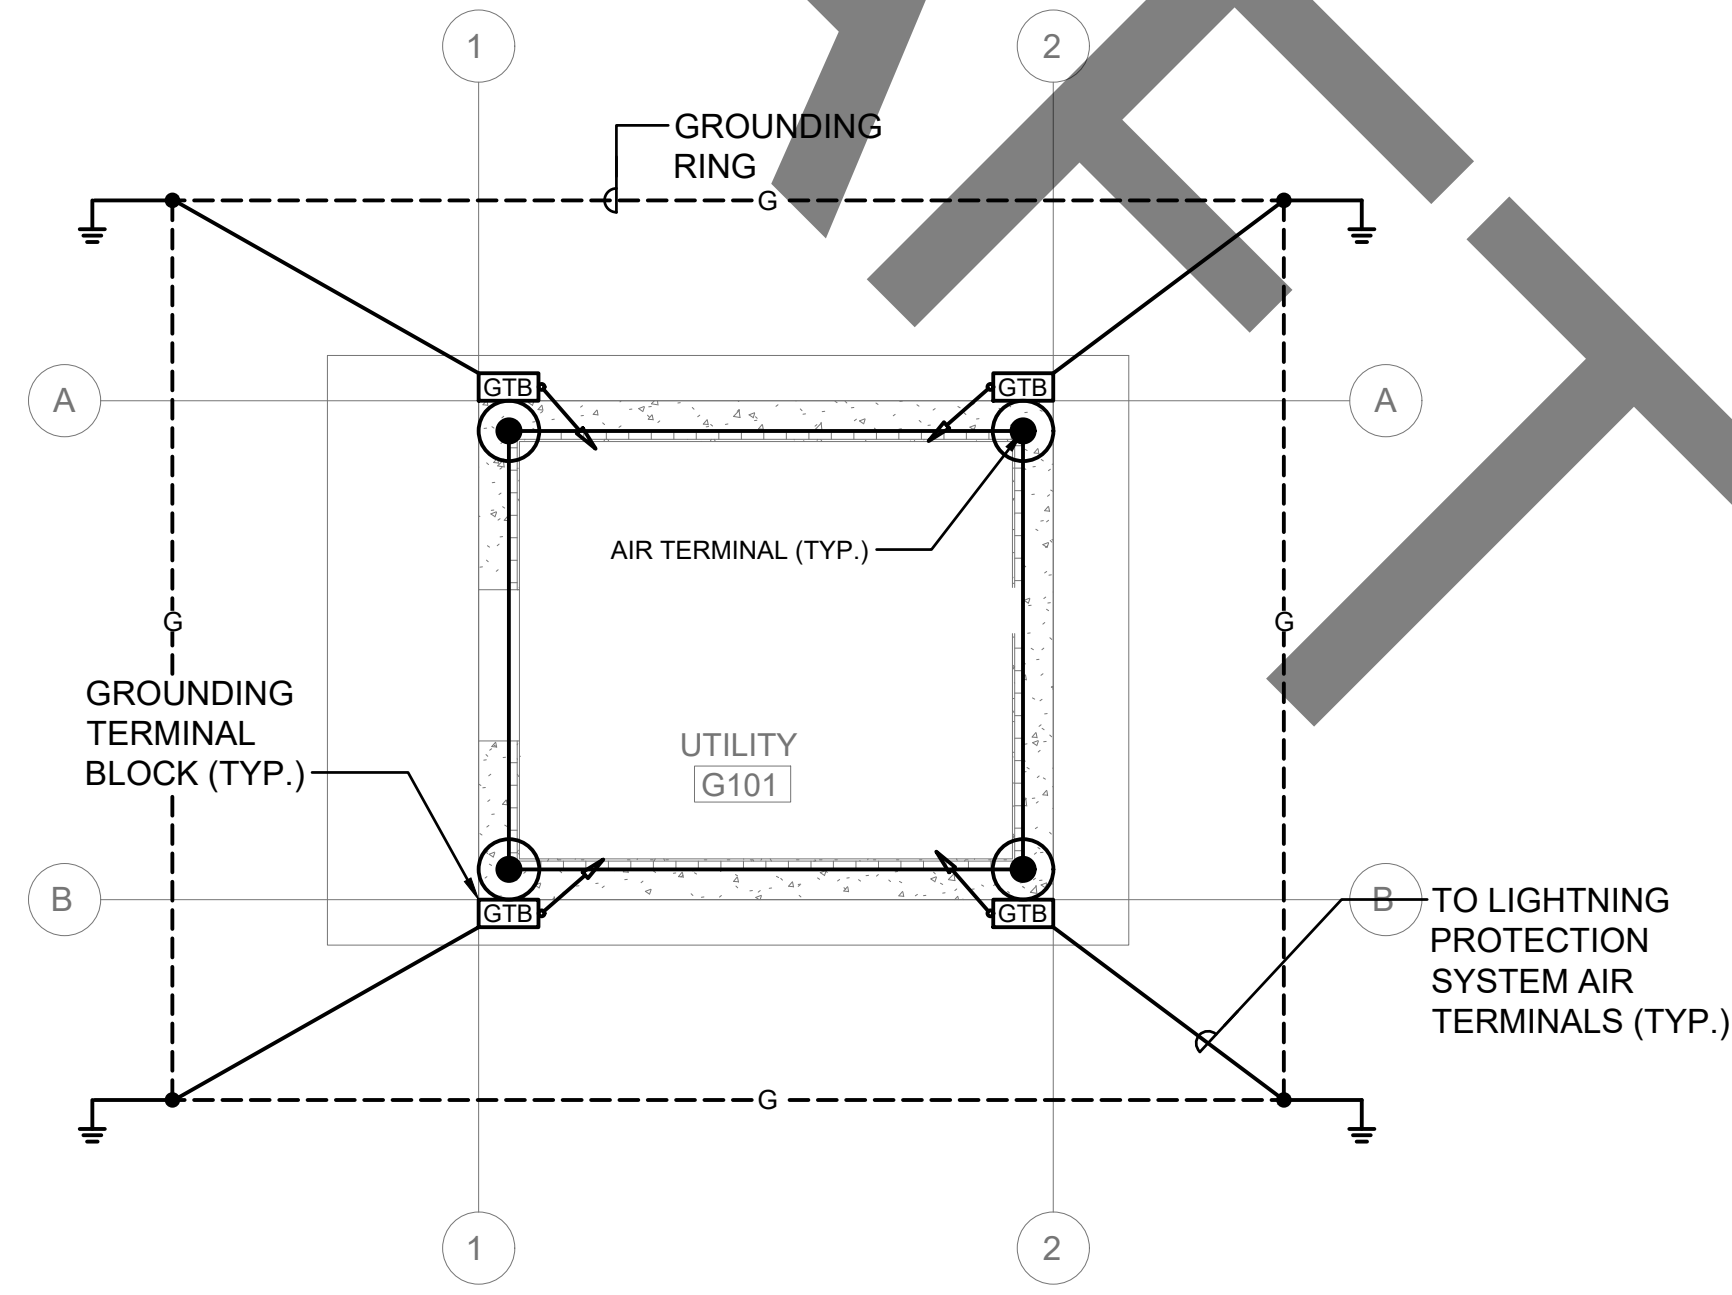

B9 CH - LIGHTNING PROTECTION PLAN (CLIN 0001)
1:50

GENERAL NOTES

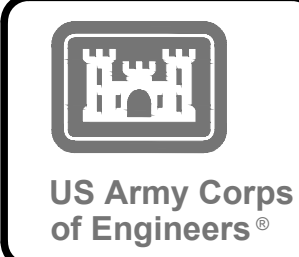

GENERAL NOTES - RCP

[illegible]

US ARMY CORPS OF ENGINEERS JAPAN DISTRICT, OKINAWA AREA OFFICE USASD-J, UNIT 35132 APO, AP 96374-5132		DESIGNED BY: DRAWN BY: CHECKED BY: SUBMITTED BY: SCALE: AS SHOWN		ISSUE DATE: SOLICITATION NO.: CONTRACT NO.: FILE NAME: 501 SUMNER STREET, SUITE 620 11	
		SSPM INTERNATIONAL, INC. 501 SUMNER STREET, SUITE 620			


LEGEND

CLIN 0001


GRAPHIC SCALE



SCALE: 1 : 50

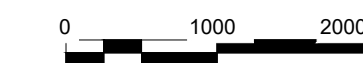

ALL DIMENSIONS AND/OR DIMENSIONS SHOWN IN
CALLOUT/ NOTES ARE IN MILLIMETERS UNLESS
OTHERWISE NOTED.

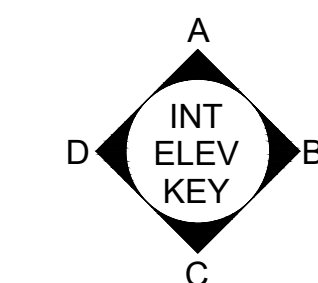


CH - POWER AND LIGHTING PLANS (CLIN 0001)

SHEET ID

EG101

INTERMEDIATE DESIGN

A

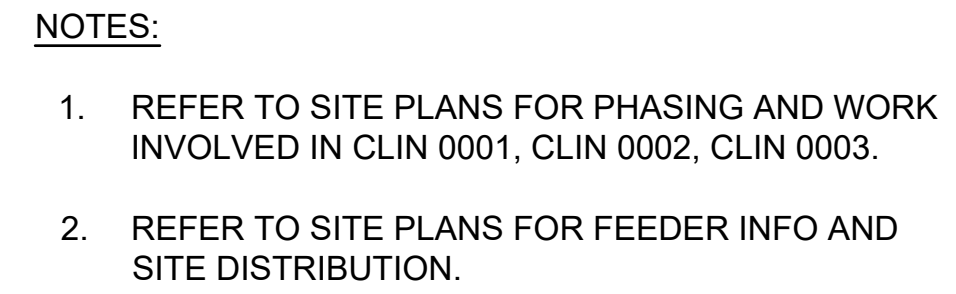

A1

CLIN 0001

G601

INTERMEDIATE DESIGN



INTERMEDIATE DESIGN


ALL DIMENSIONS AND/OR DIMENSIONS SHOWN IN
CALLOUT/ NOTES ARE IN MILLIMETERS UNLESS
OTHERWISE NOTED.

WOMEN'S TOILET

HALL
H201

19 COF SS - ENLARGED 2ND FLOOR TELECOM ROOM

1:50

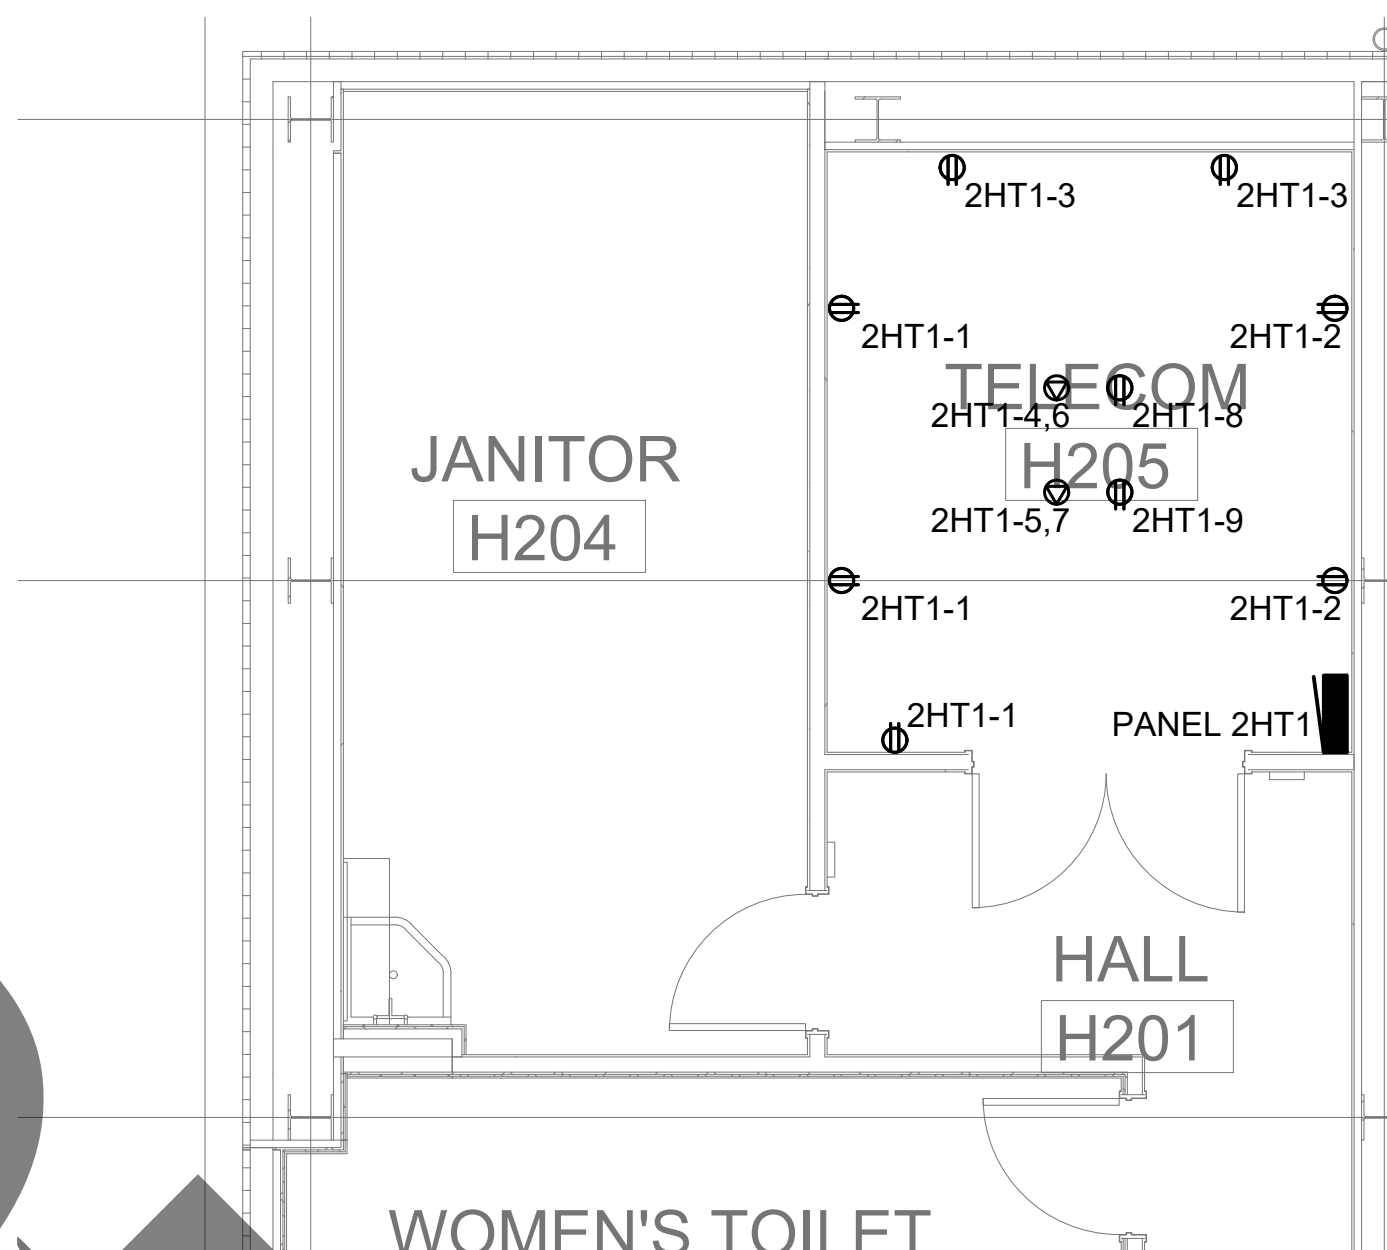

19 COF SS - ENLARGED 2ND FLOOR TELECOM ROOM
1:50

GENERAL NOTES



--	--	

US ARMY CORPS OF ENGINEERS JAPAN DISTRICT, OKINAWA AREA OFFICE USAED-J, UNIT 35132 APO, AP 96374-5132	DESIGNED BY: DRAWN BY: CHECKED BY: SUBMITTED BY: SIZE:	ISSUE DATE: SOLICITATION NO.: CONTRACT NO.: SCALE: FILE NAME:
--	--	---

KADENA AIR BASE, OKINAWA, JAPAN
VEHICLE MAINTENANCE SHOP
FY20 MCA PN77833

SHEET ID
EH40

INTERMEDIATE DESIGN


CLIN 0004

GRAPHIC SCALE




SCALE: 1 : 50

ALL DIMENSIONS AND/OR DIMENSIONS SHOWN IN
CALLOUT/ NOTES ARE IN MILLIMETERS UNLESS
OTHERWISE NOTED

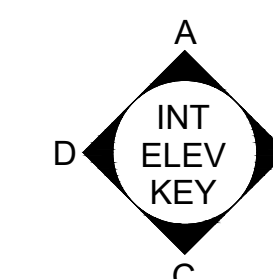

— P
— O
— N
— M
— L
— K
— J
— I
— H
— G
— F
— E
— D
— C
— B
— A

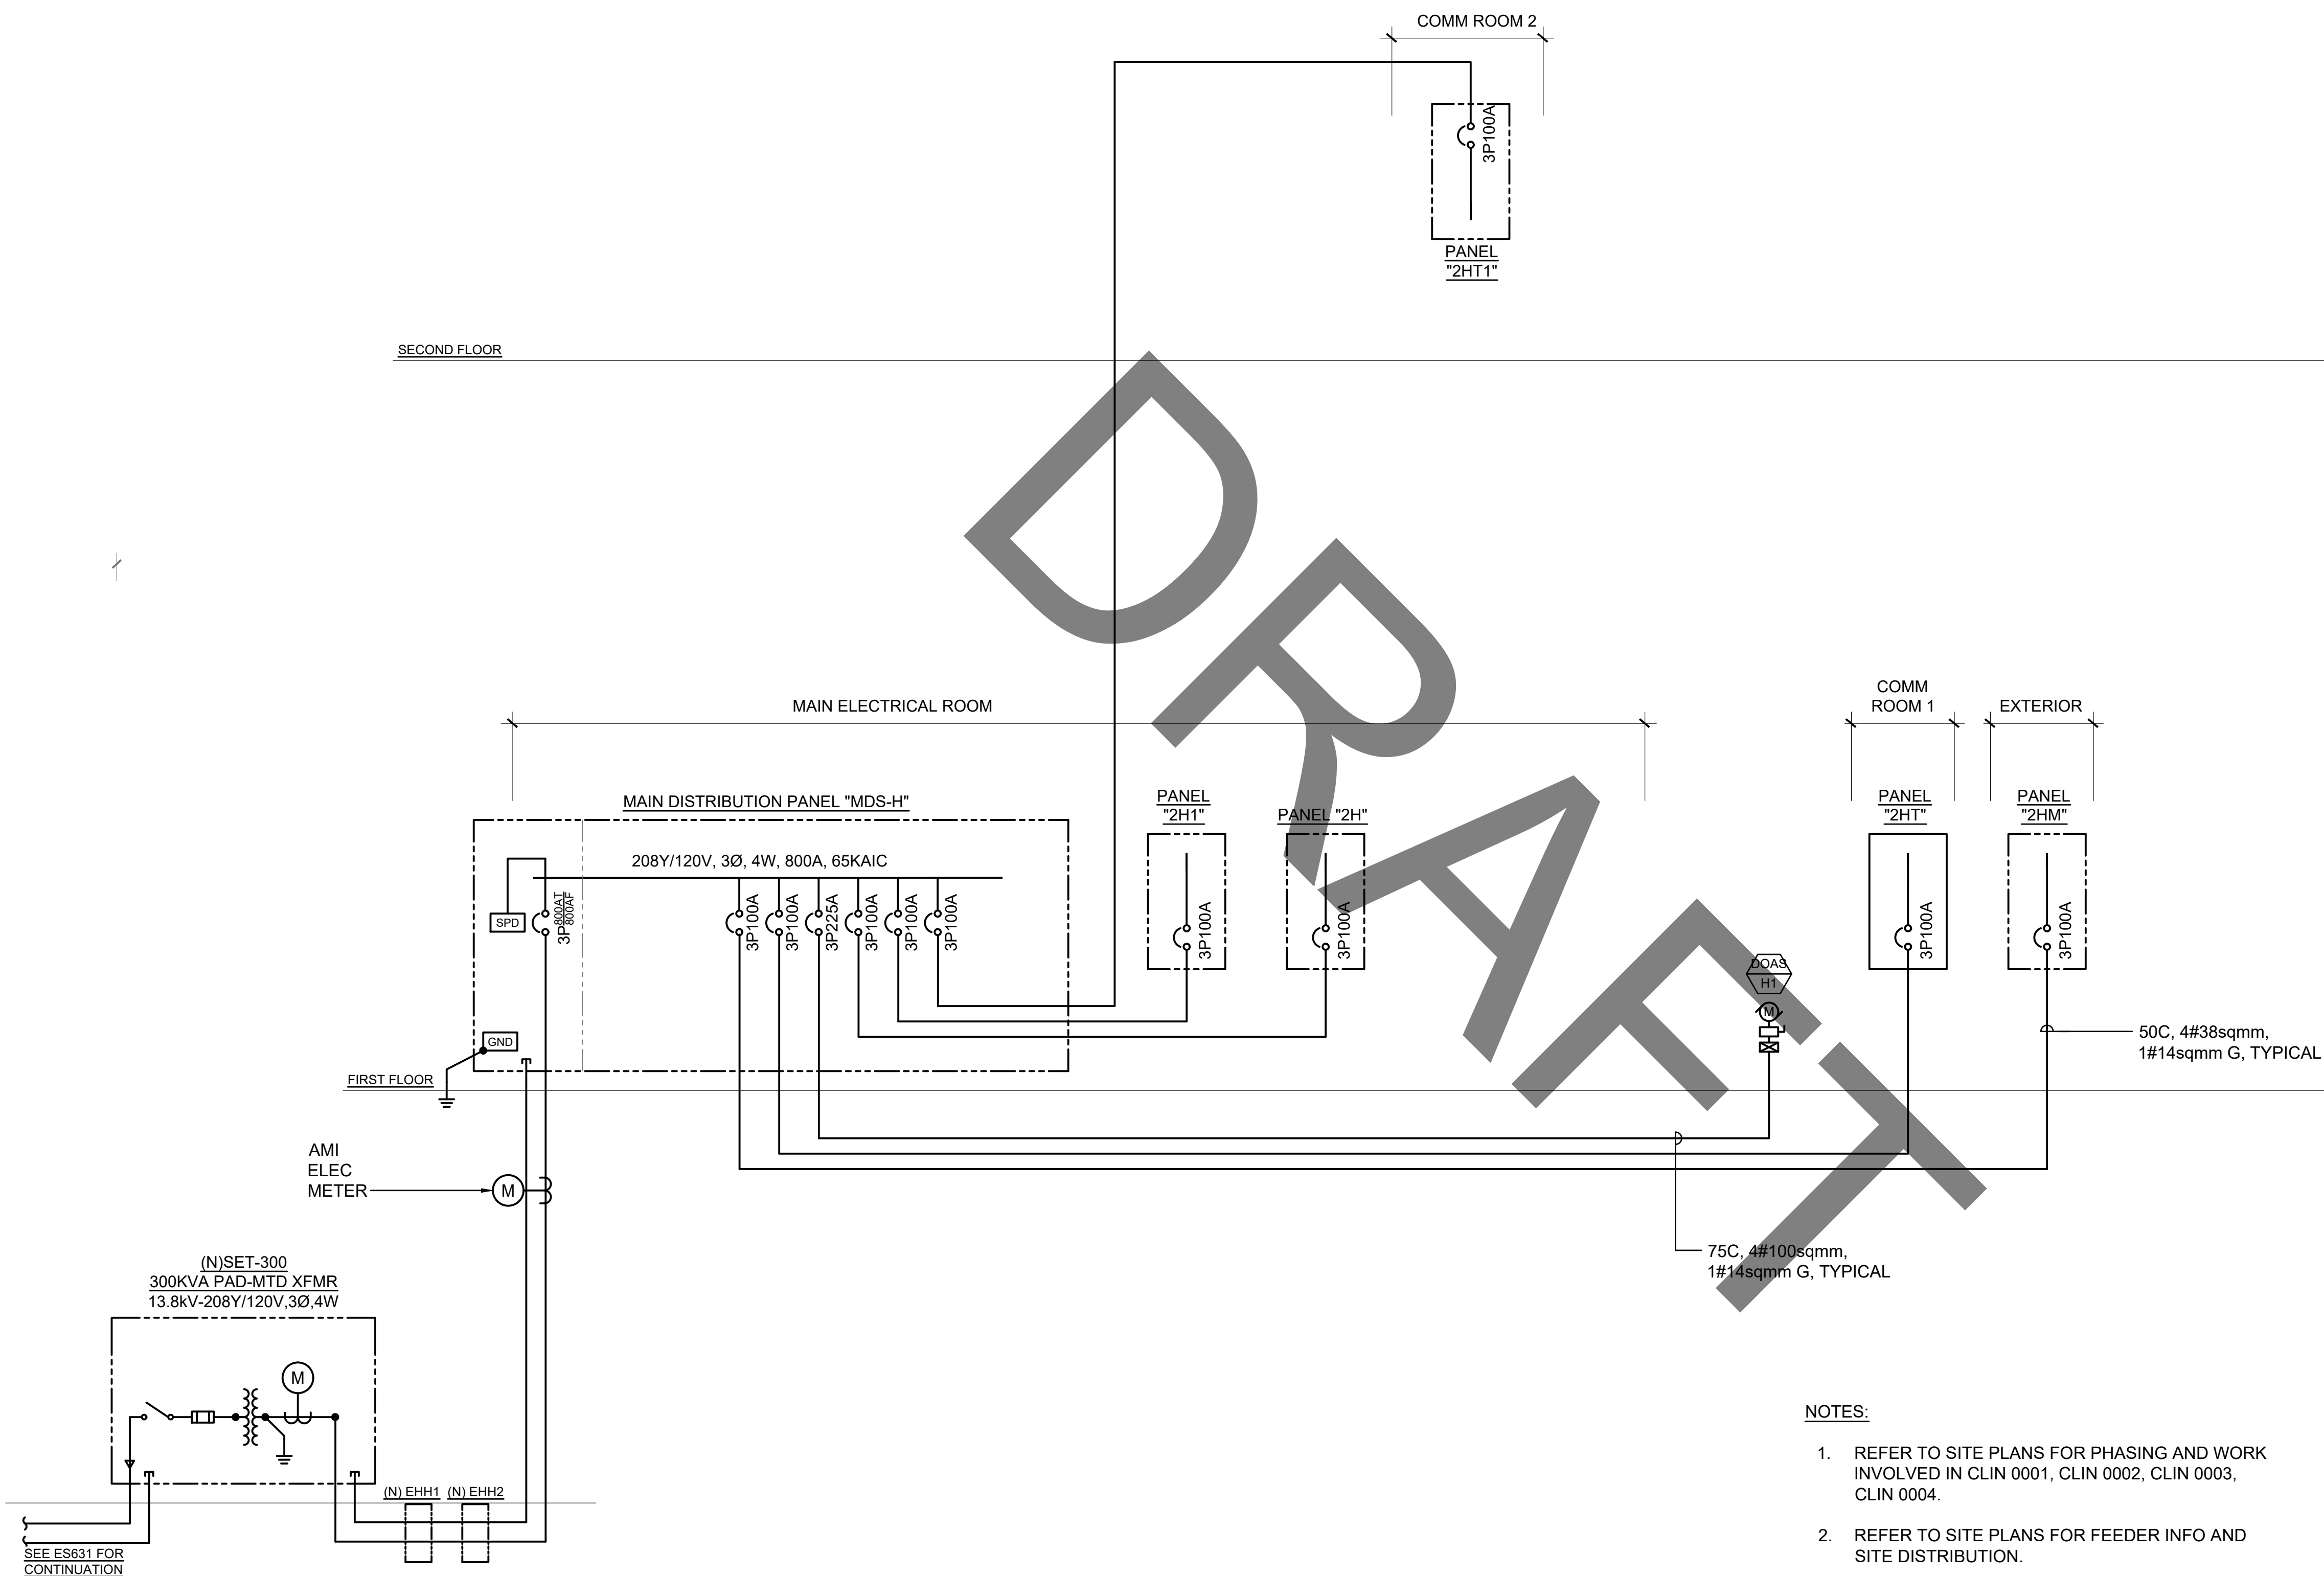

- NOTES:**
1. REFER TO SITE PLANS FOR PHASING AND WORK INVOLVED IN CLIN 0001, CLIN 0002, CLIN 0003, CLIN 0004.
 2. REFER TO SITE PLANS FOR FEEDER INFO AND SITE DISTRIBUTION.

[illegible]

USAED-J, UNIT 35132 APO, AF 96374-5132	 SSP INTERNATIONAL, INC. 501 SUMNER STREET, SUITE 620 HONOLULU, HAWAII 96817	CHECKED BY:	CONTRACT NO.:
		SUBMITTED BY:	SCALE: AS SHOWN
		SIZE:	FILE NAME:
		ISO A1	

FY20 MCA PN77833

SHEET ID
E-701


EQUIPMENT SCHEDULE										
EQUIPMENT ID	EQUIPMENT DESCRIPTION	SPECIFIED RATING (HP / KW)	SUPPLY VOLTAGE / PHASE	FLA / RLA	MOCp	MCA	TERMINATION TYPE	DISCONNECT SWITCH		REMARKS
								POLES / AMPS	ENCLOSURE	
ACCH-A1	AIR COOLED CHILLER	51.79KW	208V / 3PH		3P225A	212.4A	HARDWIRED	3P400A	NEMA 4XSS	
ACCH-D1	AIR COOLED CHILLER	23.78KW	208V / 3PH		3P110A	98.5A	HARDWIRED	3P200A	NEMA 4XSS	
AHU-A1	AIR HANDLING UNIT	11KW	208V / 3PH	30.8A	3P40A		HARDWIRED	3P60A	NEMA 1	
AHU-A2	AIR HANDLING UNIT	11KW	208V / 3PH	30.8A	3P40A		HARDWIRED	3P60A	NEMA 1	
AHU-D1	AIR HANDLING UNIT	4.6KW	208V / 3PH	12.78A	3P30A		HARDWIRED	3P30A	NEMA 1	
DOAS-A1	DEDICATED OUTSIDE AIR SYSTEM	3.8KW	208V / 3PH	10.6A	3P20A		HARDWIRED	3P30A	NEMA 4XSS	
DOAS-D1	DEDICATED OUTSIDE AIR SYSTEM	2.4KW	208V / 3PH	6.6A	3P15A		HARDWIRED	3P30A	NEMA 4XSS	
DOAS-H1	DEDICATED OUTSIDE AIR SYSTEM	41.4KW	208V / 3PH	115A	3P150A	126A	HARDWIRED	3P200A	NEMA 4XSS	
FCU-A1	FAN COIL UNIT		208V / 1PH		2P15A		HARDWIRED	2P30A	NEMA 1	PROVIDE MOTOR RATED DISCONNECT SWITCH POWERED BY ACCU
FCU-A2	FAN COIL UNIT		208V / 1PH		2P15A		HARDWIRED	2P30A	NEMA 1	PROVIDE MOTOR RATED DISCONNECT SWITCH POWERED BY ACCU
FCU-A3	FAN COIL UNIT		208V / 1PH		2P15A		HARDWIRED	2P30A	NEMA 1	PROVIDE MOTOR RATED DISCONNECT SWITCH POWERED BY ACCU
FCU-A4	FAN COIL UNIT		208V / 1PH		2P15A		HARDWIRED	2P30A	NEMA 1	PROVIDE MOTOR RATED DISCONNECT SWITCH POWERED BY ACCU
FCU-A5	FAN COIL UNIT		208V / 1PH		2P15A		HARDWIRED	2P30A	NEMA 1	PROVIDE MOTOR RATED DISCONNECT SWITCH POWERED BY ACCU
FCU-A6	FAN COIL UNIT		208V / 1PH		2P15A		HARDWIRED	2P30A	NEMA 1	PROVIDE MOTOR RATED DISCONNECT SWITCH POWERED BY ACCU
FCU-B1	FAN COIL UNIT		208V / 1PH		2P15A		HARDWIRED	2P30A	NEMA 1	PROVIDE MOTOR RATED DISCONNECT SWITCH POWERED BY ACCU
FCU-B2	FAN COIL UNIT		208V / 1PH		2P15A		HARDWIRED	2P30A	NEMA 1	PROVIDE MOTOR RATED DISCONNECT SWITCH POWERED BY ACCU
FCU-B3	FAN COIL UNIT		208V / 1PH		2P15A		HARDWIRED	2P30A	NEMA 1	PROVIDE MOTOR RATED DISCONNECT SWITCH POWERED BY ACCU
FCU-B4	FAN COIL UNIT		208V / 1PH		2P15A		HARDWIRED	2P30A	NEMA 1	PROVIDE MOTOR RATED DISCONNECT SWITCH POWERED BY ACCU
FCU-B5	FAN COIL UNIT		208V / 1PH		2P15A		HARDWIRED	2P30A	NEMA 1	PROVIDE MOTOR RATED DISCONNECT SWITCH POWERED BY ACCU
FCU-B6	FAN COIL UNIT		208V / 1PH		2P15A		HARDWIRED	2P30A	NEMA 1	PROVIDE MOTOR RATED DISCONNECT SWITCH POWERED BY ACCU
FCU-D1	FAN COIL UNIT		208V / 1PH		2P15A		HARDWIRED	2P30A	NEMA 1	PROVIDE MOTOR RATED DISCONNECT SWITCH POWERED BY ACCU
FCU-D2	FAN COIL UNIT		208V / 1PH		2P15A		HARDWIRED	2P30A	NEMA 1	PROVIDE MOTOR RATED DISCONNECT SWITCH POWERED BY ACCU
FCU-G1	FAN COIL UNIT		208V / 1PH		2P15A		HARDWIRED	2P30A	NEMA 1	PROVIDE MOTOR RATED DISCONNECT SWITCH POWERED BY ACCU

EQUIPMENT SCHEDULE										
EQUIPMENT ID	EQUIPMENT DESCRIPTION	SPECIFIED RATING (HP / KW)	SUPPLY VOLTAGE / PHASE	FLA / RLA	MOCp	MCA	TERMINATION TYPE	DISCONNECT SWITCH		REMARKS
								POLES / AMPS	ENCLOSURE	
FCU-H1	FAN COIL UNIT		208V / 1PH		2P15A		HARDWIRED	2P30A	NEMA 1	PROVIDE MOTOR RATED DISCONNECT SWITCH POWERED BY ACCU
FCU-H2	FAN COIL UNIT		208V / 1PH		2P15A		HARDWIRED	2P30A	NEMA 1	PROVIDE MOTOR RATED DISCONNECT SWITCH POWERED BY ACCU
FCU-H3	FAN COIL UNIT		208V / 1PH		2P15A		HARDWIRED	2P30A	NEMA 1	PROVIDE MOTOR RATED DISCONNECT SWITCH POWERED BY ACCU
FCU-H4	FAN COIL UNIT		208V / 1PH		2P15A		HARDWIRED	2P30A	NEMA 1	PROVIDE MOTOR RATED DISCONNECT SWITCH POWERED BY ACCU
FCU-H5	FAN COIL UNIT		208V / 1PH		2P15A		HARDWIRED	2P30A	NEMA 1	PROVIDE MOTOR RATED DISCONNECT SWITCH POWERED BY ACCU
FCU-H6	FAN COIL UNIT		208V / 1PH		2P15A		HARDWIRED	2P30A	NEMA 1	PROVIDE MOTOR RATED DISCONNECT SWITCH POWERED BY ACCU
FCU-H7	FAN COIL UNIT		208V / 1PH		2P15A		HARDWIRED	2P30A	NEMA 1	PROVIDE MOTOR RATED DISCONNECT SWITCH POWERED BY ACCU
FCU-H8	FAN COIL UNIT		208V / 1PH		2P15A		HARDWIRED	2P30A	NEMA 1	PROVIDE MOTOR RATED DISCONNECT SWITCH POWERED BY ACCU
FCU-H9	FAN COIL UNIT		208V / 1PH		2P15A		HARDWIRED	2P30A	NEMA 1	PROVIDE MOTOR RATED DISCONNECT SWITCH POWERED BY ACCU
FCU-H10	FAN COIL UNIT		208V / 1PH		2P15A		HARDWIRED	2P30A	NEMA 1	PROVIDE MOTOR RATED DISCONNECT SWITCH POWERED BY ACCU
FCU-H11	FAN COIL UNIT		208V / 1PH		2P15A		HARDWIRED	2P30A	NEMA 1	PROVIDE MOTOR RATED DISCONNECT SWITCH POWERED BY ACCU
FCU-H12	FAN COIL UNIT		208V / 1PH		2P15A		HARDWIRED	2P30A	NEMA 1	PROVIDE MOTOR RATED DISCONNECT SWITCH POWERED BY ACCU
ACCU-A1	AIR COOLED CONDENSING UNIT	1.52KW	208V / 1PH	8.09A	2P15A		HARDWIRED	2P30A	NEMA 4XSS	
ACCU-A2	AIR COOLED CONDENSING UNIT	1.06KW	208V / 1PH	5.82A	2P15A		HARDWIRED	2P30A	NEMA 4XSS	
ACCU-A3	AIR COOLED CONDENSING UNIT	1.52KW	208V / 1PH	8.09A	2P15A		HARDWIRED	2P30A	NEMA 4XSS	
ACCU-A4	AIR COOLED CONDENSING UNIT	1.61KW	208V / 1PH	8.56A	2P15A		HARDWIRED	2P30A	NEMA 4XSS	
ACCU-A5	AIR COOLED CONDENSING UNIT	1.61KW	208V / 1PH	8.56A	2P15A		HARDWIRED	2P30A	NEMA 4XSS	
ACCU-A6	AIR COOLED CONDENSING UNIT	1.52KW	208V / 1PH	8.09A	2P15A		HARDWIRED	2P30A	NEMA 4XSS	
ACCU-B1	AIR COOLED CONDENSING UNIT	1.61KW	208V / 1PH	8.56A	2P15A		HARDWIRED	2P30A	NEMA 4XSS	
ACCU-B2	AIR COOLED CONDENSING UNIT	1.61KW	208V / 1PH	8.56A	2P15A		HARDWIRED	2P30A	NEMA 4XSS	
ACCU-B3	AIR COOLED CONDENSING UNIT	1.61KW	208V / 1PH	8.56A	2P15A		HARDWIRED	2P30A	NEMA 4XSS	
ACCU-B4	AIR COOLED CONDENSING UNIT	1.61KW	208V / 1PH	8.56A	2P15A		HARDWIRED	2P30A	NEMA 4XSS	
ACCU-B5	AIR COOLED CONDENSING UNIT	1.61KW	208V / 1PH	8.56A	2P15A		HARDWIRED	2P30A	NEMA 4XSS	
ACCU-B6	AIR COOLED CONDENSING UNIT	1.61KW	208V / 1PH	8.56A	2P15A		HARDWIRED	2P30A	NEMA 4XSS	
ACCU-D1	AIR COOLED CONDENSING UNIT	1.06KW	208V / 1PH	5.82A	2P15A		HARDWIRED	2P30A	NEMA 4XSS	
ACCU-D2	AIR COOLED CONDENSING UNIT	1.52KW	208V / 1PH	8.09A	2P15A		HARDWIRED	2P30A	NEMA 4XSS	
ACCU-G1	AIR COOLED CONDENSING UNIT	1.61KW	208V / 1PH	8.56A	2P15A		HARDWIRED	2P30A	NEMA 4XSS	

P
O
N
M
L
K
J
I
H
G
F
E
D
C
B
A

EQUIPMENT SCHEDULE										
EQUIPMENT ID	EQUIPMENT DESCRIPTION	SPECIFIED RATING (HP / KW)	SUPPLY VOLTAGE / PHASE	FLA / RLA	MOC	MCA	TERMINATION TYPE	DISCONNECT SWITCH		REMARKS
								POLES / AMPS	ENCLOSURE	
ACCU-H1	AIR COOLED CONDENSING UNIT	1.06KW	208V / 1PH	5.82A	2P20A	13.1A	HARDWIRED	2P30A	NEMA 4XSS	
ACCU-H2	AIR COOLED CONDENSING UNIT	2.16KW	208V / 1PH	11.5A	2P20A	14.9A	HARDWIRED	2P30A	NEMA 4XSS	
ACCU-H3	AIR COOLED CONDENSING UNIT	1.06KW	208V / 1PH	5.82A	2P20A	13.1A	HARDWIRED	2P30A	NEMA 4XSS	
ACCU-H4	AIR COOLED CONDENSING UNIT	1.61KW	208V / 1PH	8.56A	2P20A	13.3A	HARDWIRED	2P30A	NEMA 4XSS	
ACCU-H5	AIR COOLED CONDENSING UNIT	1.61KW	208V / 1PH	8.56A	2P20A	13.3A	HARDWIRED	2P30A	NEMA 4XSS	
ACCU-H6	AIR COOLED CONDENSING UNIT	1.61KW	208V / 1PH	8.56A	2P20A	13.3A	HARDWIRED	2P30A	NEMA 4XSS	
ACCU-H7	AIR COOLED CONDENSING UNIT	1.06KW	208V / 1PH	5.82A	2P20A	13.1A	HARDWIRED	2P30A	NEMA 4XSS	
ACCU-H8	AIR COOLED CONDENSING UNIT	1.61KW	208V / 1PH	8.56A	2P20A	13.3A	HARDWIRED	2P30A	NEMA 4XSS	
ACCU-H9	AIR COOLED CONDENSING UNIT	1.61KW	208V / 1PH	8.56A	2P20A	13.3A	HARDWIRED	2P30A	NEMA 4XSS	
ACCU-H10	AIR COOLED CONDENSING UNIT	1.61KW	208V / 1PH	8.56A	2P20A	13.3A	HARDWIRED	2P30A	NEMA 4XSS	
ACCU-H11	AIR COOLED CONDENSING UNIT	1.61KW	208V / 1PH	8.56A	2P20A	13.3A	HARDWIRED	2P30A	NEMA 4XSS	
ACCU-H12	AIR COOLED CONDENSING UNIT	2.16KW	208V / 1PH	11.5A	2P20A	14.9A	HARDWIRED	2P30A	NEMA 4XSS	
EF-A1.1	EXHAUST FAN	0.1875KW	120V / 1PH	1.9A	1P15A		HARDWIRED	1P30A	NEMA 1	PROVIDE MOTOR RATED DISCONNECT SWITCH PROVIDE120V-100V STEP DOWN TRANSFORMER
EF-A1.2	EXHAUST FAN	0.05KW	120V / 1PH	0.84A	1P15A		HARDWIRED	1P30A	NEMA 1	PROVIDE MOTOR RATED DISCONNECT SWITCH PROVIDE120V-100V STEP DOWN TRANSFORMER
EF-A1.3	EXHAUST FAN	0.1875KW	120V / 1PH	1.9A	1P15A		HARDWIRED	1P30A	NEMA 1	PROVIDE MOTOR RATED DISCONNECT SWITCH PROVIDE120V-100V STEP DOWN TRANSFORMER
EF-A1.4	EXHAUST FAN	23.125KW	208V / 3PH	69A	3P125A		HARDWIRED	3P200A	NEMA 1	
EF-A1.5	EXHAUST FAN	6.875KW	208V / 3PH	21.4A	3P40A		HARDWIRED	3P60A	NEMA 1	
EF-A1.6	EXHAUST FAN	2.7KW	208V / 3PH	7.5A	3P15A	9.4A	HARDWIRED	3P30A	NEMA 1	
EF-A1.7	EXHAUST FAN	2.7KW	208V / 3PH	7.5A	3P15A	9.4A	HARDWIRED	3P30A	NEMA 1	
EF-A1.8	EXHAUST FAN	2.7KW	208V / 3PH	7.5A	3P15A	9.4A	HARDWIRED	3P30A	NEMA 1	
EF-A1.9	EXHAUST FAN	2.7KW	208V / 3PH	7.5A	3P15A	9.4A	HARDWIRED	3P30A	NEMA 1	
EF-A1.10	EXHAUST FAN	2.7KW	208V / 3PH	7.5A	3P15A	9.4A	HARDWIRED	3P30A	NEMA 1	
EF-A1.11	EXHAUST FAN	2.7KW	208V / 3PH	7.5A	3P15A	9.4A	HARDWIRED	3P30A	NEMA 1	
EF-A1.12	EXHAUST FAN	2.7KW	208V / 3PH	7.5A	3P15A	9.4A	HARDWIRED	3P30A	NEMA 1	
EF-A1.13	EXHAUST FAN	0.187KW	208V / 1PH	0.9A	2P15A	1.1A	HARDWIRED	2P30A	NEMA 1	PROVIDE MOTOR RATED DISCONNECT SWITCH PROVIDE120V-100V STEP DOWN TRANSFORMER
EA-A2.1	EXHAUST FAN	0.015KW	120V / 1PH	0.42A	1P15A		HARDWIRED	1P30A	NEMA 1	PROVIDE MOTOR RATED DISCONNECT SWITCH PROVIDE120V-100V STEP DOWN TRANSFORMER
EA-A2.2	EXHAUST FAN	0.05KW	120V / 1PH	0.84A	1P15A		HARDWIRED	1P30A	NEMA 1	PROVIDE MOTOR RATED DISCONNECT SWITCH PROVIDE120V-100V STEP DOWN TRANSFORMER

EQUIPMENT SCHEDULE										
EQUIPMENT ID	EQUIPMENT DESCRIPTION	SPECIFIED RATING (HP / KW)	SUPPLY VOLTAGE / PHASE	FLA / RLA	MOC	MCA	TERMINATION TYPE	DISCONNECT SWITCH		REMARKS
								POLES / AMPS	ENCLOSURE	
EF-B1	EXHAUST FAN	0.47KW	120V / 1PH	4.7A	1P15A		HARDWIRED	2P30A	NEMA 1	PROVIDE MOTOR RATED DISCONNECT SWITCH PROVIDE120V-100V STEP DOWN TRANSFORMER
EF-B2	EXHAUST FAN	0.47KW	120V / 1PH	4.7A	1P15A		HARDWIRED	2P30A	NEMA 1	PROVIDE MOTOR RATED DISCONNECT SWITCH PROVIDE120V-100V STEP DOWN TRANSFORMER
EF-B3	EXHAUST FAN	0.47KW	120V / 1PH	4.7A	1P15A		HARDWIRED	2P30A	NEMA 1	PROVIDE MOTOR RATED DISCONNECT SWITCH PROVIDE120V-100V STEP DOWN TRANSFORMER
EF-B4	EXHAUST FAN	0.47KW	120V / 1PH	4.7A	1P15A		HARDWIRED	2P30A	NEMA 1	PROVIDE MOTOR RATED DISCONNECT SWITCH PROVIDE120V-100V STEP DOWN TRANSFORMER
EF-B5	EXHAUST FAN	0.47KW	120V / 1PH	4.7A	1P15A		HARDWIRED	2P30A	NEMA 1	PROVIDE MOTOR RATED DISCONNECT SWITCH PROVIDE120V-100V STEP DOWN TRANSFORMER
EF-B6	EXHAUST FAN	0.47KW	120V / 1PH	4.7A	1P15A		HARDWIRED	2P30A	NEMA 1	PROVIDE MOTOR RATED DISCONNECT SWITCH PROVIDE120V-100V STEP DOWN TRANSFORMER
EF-C1	EXHAUST FAN	0.57KW	208V / 3PH	2.4A	3P15A		HARDWIRED	2P30A	NEMA 1	
EF-C2	EXHAUST FAN	0.57KW	208V / 3PH	2.4A	3P15A		HARDWIRED	2P30A	NEMA 1	
EF-D1	EXHAUST FAN	0.0175KW	120V / 1PH	1.46A	1P15A		HARDWIRED	1P30A	NEMA 1	PROVIDE MOTOR RATED DISCONNECT SWITCH PROVIDE120V-100V STEP DOWN TRANSFORMER
EF-D2	EXHAUST FAN	0.05KW	120V / 1PH	0.84A	1P15A		HARDWIRED	1P30A	NEMA 1	PROVIDE MOTOR RATED DISCONNECT SWITCH PROVIDE120V-100V STEP DOWN TRANSFORMER
EF-D3	EXHAUST FAN	0.05KW	120V / 1PH	0.84A	1P15A		HARDWIRED	1P30A	NEMA 1	PROVIDE MOTOR RATED DISCONNECT SWITCH PROVIDE120V-100V STEP DOWN TRANSFORMER
EF-D4	EXHAUST FAN	0.05KW	120V / 1PH	0.84A	1P15A		HARDWIRED	1P30A	NEMA 1	PROVIDE MOTOR RATED DISCONNECT SWITCH PROVIDE120V-100V STEP DOWN TRANSFORMER
EF-D5.1	EXHAUST FAN	2.75KW	208V / 3PH	9.4A	3P20A		HARDWIRED	3P30A	NEMA 1	
EF-D5.2	EXHAUST FAN	2.75KW	208V / 3PH	9.4A	3P20A		HARDWIRED	3P30A	NEMA 1	
EF-D5.3	EXHAUST FAN	2.75KW	208V / 3PH	9.4A	3P20A		HARDWIRED	3P30A	NEMA 1	
EF-D6	EXHAUST FAN	0.875KW	208V / 3PH	2.8A	3P15A		HARDWIRED	3P30A	NEMA 1	
EF-D7	EXHAUST FAN	0.05KW	120V / 1PH	0.84A	1P15A		HARDWIRED	1P30A	NEMA 1	PROVIDE MOTOR RATED DISCONNECT SWITCH PROVIDE120V-100V STEP DOWN TRANSFORMER
EF-F1	EXHAUST FAN	0.05KW	120V / 1PH	0.84A	1P15A		HARDWIRED	2P30A	NEMA 4XSS	PROVIDE MOTOR RATED DISCONNECT SWITCH PROVIDE 120V-100V STEP DOWN TRANSFORMER
EF-H1	EXHAUST FAN	0.05KW	120V / 1PH	0.84A	1P15A		HARDWIRED	1P30A	NEMA 1	PROVIDE MOTOR RATED DISCONNECT SWITCH. PROVIDE120V-100V STEP DOWN TRANSFORMER
EF-H2	EXHAUST FAN	0.015KW	120V / 1PH	0.42A	1P15A		HARDWIRED	1P30A	NEMA 1	PROVIDE MOTOR RATED DISCONNECT SWITCH. PROVIDE120V-100V STEP DOWN TRANSFORMER
EF-H3	EXHAUST FAN	0.03KW	120V / 1PH	0.64A	1P15A		HARDWIRED	1P30A	NEMA 1	PROVIDE MOTOR RATED DISCONNECT SWITCH. PROVIDE120V-100V STEP DOWN TRANSFORMER
EF-H4	EXHAUST FAN	0.03KW	120V / 1PH	0.64A	1P15A		HARDWIRED	1P30A	NEMA 1	PROVIDE MOTOR RATED DISCONNECT SWITCH. PROVIDE120V-100V STEP DOWN TRANSFORMER
EF-H5	EXHAUST FAN	0.1KW	120V / 1PH	1.8A	1P15A		HARDWIRED	1P30A	NEMA 1	PROVIDE MOTOR RATED DISCONNECT SWITCH. PROVIDE120V-100V STEP DOWN TRANSFORMER
EF-H6	EXHAUST FAN	0.015KW	120V / 1PH	0.42A	1P15A		HARDWIRED	1P30A	NEMA 1	PROVIDE MOTOR RATED DISCONNECT SWITCH. PROVIDE120V-100V STEP DOWN TRANSFORMER
EF-H7	EXHAUST FAN	0.03KW	120V / 1PH	0.64A	1P15A		HARDWIRED	1P30A	NEMA 1	PROVIDE MOTOR RATED DISCONNECT SWITCH. PROVIDE120V-100V STEP DOWN TRANSFORMER
EF-H8	EXHAUST FAN	0.03KW	120V / 1PH	0.64A	1P15A		HARDWIRED	1P30A	NEMA 1	PROVIDE MOTOR RATED DISCONNECT SWITCH. PROVIDE120V-100V STEP DOWN TRANSFORMER
EF-H9	EXHAUST FAN	0.015KW	120V / 1PH	0.42A	1P15A		HARDWIRED	1P30A	NEMA 1	PROVIDE MOTOR RATED DISCONNECT SWITCH. PROVIDE120V-100V STEP DOWN TRANSFORMER

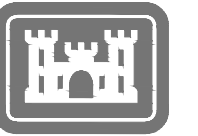

US Army Corps
of Engineers®

DESIGNED BY:
JAPAN DISTRICT, OKINAWA AREA OFFICE
USAED-J UNIT 35132
APO, AP 96374-5132

ISSUE DATE:
SOLICITATION NO.:
CONTRACT NO.:
SCALE:
AS SHOWN

FILE NAME:
ISO A1

US ARMY CORPS OF ENGINEERS
JAPAN DISTRICT, OKINAWA AREA OFFICE
USAED-J UNIT 35132
APO, AP 96374-5132



SSEW INTERNATIONAL, INC.
501 SUMNER STREET, SUITE 620
HONOLULU, HAWAII 96817

KADENA AIR BASE, OKINAWA, JAPAN
VEHICLE MAINTENANCE SHOP
FY20 MCA PN77833

EQUIPMENT SCHEDULES

SHEET ID

E-702

INTERMEDIATE DESIGN

P

O

N

M

L

K

J

1

H

G

F

E

D

C

B

A

EQUIPMENT ID	EQUIPMENT DESCRIPTION	SPECIFIED RATING (HP / KW)	SUPPLY VOLTAGE / PHASE	FLA / RLA	MOCBP	MCA	TERMINATION TYPE	DISCONNECT SWITCH		REMARKS
								POLES / AMPS	ENCLOSURE	
HVLS-D1	HIGH VOLUME LOW SPEED FAN	1.26KW	208V / 3PH	3.5A	3P15A		HARDWIRED	3P30A	NEMA 1	
HVLS-D2	HIGH VOLUME LOW SPEED FAN	1.26KW	208V / 3PH	3.5A	3P15A		HARDWIRED	3P30A	NEMA 1	
HVLS-D3	HIGH VOLUME LOW SPEED FAN	1.26KW	208V / 3PH	3.5A	3P15A		HARDWIRED	3P30A	NEMA 1	
HVLS-D4	HIGH VOLUME LOW SPEED FAN	1.26KW	208V / 3PH	3.5A	3P15A		HARDWIRED	3P30A	NEMA 1	
MAF-A1	MAKEUP AIR FAN	21.38KW	208V / 3PH	59.4A	3P100A		HARDWIRED	3P100A	NEMA 1	
VAV			120V / 1PH		1P15A		HARDWIRED			PROVIDE MOTOR RATED DISCONNECT SWITCH PROVIDE 120V-24V STEP DOWN TRANSFORMER
AC-A1	AIR COMPRESSOR	46.25KW	208V / 3PH	128.5A	3P225A		HARDWIRED	3P400A	NEMA 1	
HPWH-A1	HYBRID ELECTRIC HEAT PUMP WATER HEATER	1.2KW	100V / 1PH	12A	1P20A		HARDWIRED	1P30A	NEMA 1	PROVIDE 120V-100V STEP DOWN TRANSFORMER
PW-I1	PRESSURE WASHER	8.64KW	208V / 3PH	30A	3P30A		HARDWIRED	3P30A	NEMA 4XSS	
PW-I2	PRESSURE WASHER	8.64KW	208V / 3PH	30A	3P30A		HARDWIRED	3P30A	NEMA 4XSS	
PW-I3	PRESSURE WASHER	8.64KW	208V / 3PH	30A	3P30A		HARDWIRED	3P30A	NEMA 4XSS	
WWRS-I1	RECYCLING SYSTEM	11.52KW	208V / 3PH	40A	3P40A		HARDWIRED	3P60A	NEMA 4XSS	
WWRS-I2	RECYCLING SYSTEM	11.52KW	208V / 3PH	40A	3P40A		HARDWIRED	3P60A	NEMA 4XSS	
WWRS-I3	RECYCLING SYSTEM	11.52KW	208V / 3PH	40A	3P40A		HARDWIRED	3P60A	NEMA 4XSS	
SP-A1	SUMP PUMP	0.94KW	208V / 3PH	3.4A	3P15A		HARDWIRED	3P30A	NEMA 4XSS	
SP-A2	SUMP PUMP	1.875KW	208V / 3PH	5.2A	3P15A		HARDWIRED	3P30A	NEMA 4XSS	



U.S. Army Corps
Engineers®

[illegible]

JAPAN DISTRICT, OKINAWA AREA OFFICE				SSPM INTERNATIONAL, INC. 501 KALANIANAʻOHE BLVD #20 HONOLULU, HAWAII 96817	
DRAWN BY:		SOLICITATION NO.:			
CHECKED BY:		CONTRACT NO.:			
SUBMITTED BY:		SCALE:		AS SHOWN	
SIZE:		FILE NAME:			
ISO A1					

VEHICLE MAINTENANCE SHOP
FY20 MCA PN77833

SHEET ID

E-703


INTERMEDIATE DESIGN

DRAWN BY: USAED-J, UNIT 35132 APO, AP 96374-5132	 SFSM INTERNATIONAL, INC. SUMNER STREET, SUITE 620 HONOLULU, HAWAII 96817	CONTRACT NO.: SCALE: AS SHOWN
CHECKED BY: SUBMITTED BY:	SIZE:	FILE NAME:
	ISO A1	

SHEET ID
E-711

PANEL: "2A4"			VOLTAGE: 208Y/120V			3 PHASE			POLES: 3			42		
MAIN BUS: 225A			MAIN BKR: 3P225A			4 WIRE			MIN. A.I.C.: 20"			65,000		
MOUNTING: SURFACE			BKR TYPE: BOLT-ON						CABINET WIDTH: 20"					
WIRE	CKT NO.	DESCRIPTION	CKT BKR	KVA			C	CKT BKR	DESCRIPTION	CKT NO.	WIRE			
				A	B									
2	1	R - A101 PLATFORM	1P20A	0.5	1.0			1P20A	L - A101	2	2			
2	3	R - A101	1P20A		0.9	1.0		1P20A	L - A101	4	2			
2	5	R - A101	1P20A				1.1	0.5	1P20A	ROLL UP DOOR	6	2		
2	7	R - A101	1P20A	0.5	0.5			1P20A	ROLL UP DOOR	8	2			
2	9	R - A101	1P20A		0.2	0.5		1P20A	ROLL UP DOOR	10	2			
2	11	R - A101	1P20A				0.2	0.5	1P20A	ROLL UP DOOR	12	2		
2	13	R - A101	1P20A	0.2	1.9			3P20A	R - BATTERY CHARGING	14	2			
2	15	R - EXTERIOR	1P20A		0.5	1.9		-	PART OF CIRCUIT 14	16	2			
2	17	R - BATTERY CHARGING	3P20A				1.9	1.9	-	PART OF CIRCUIT 14	18	2		
2	19	PART OF CIRCUIT 17	-	1.9	1.9			3P20A	R - BATTERY CHARGING	20	2			
2	21	PART OF CIRCUIT 17	-		1.9	1.9		-	PART OF CIRCUIT 20	22	2			
2	23	R - BATTERY CHARGING	3P20A				1.9	1.9	-	PART OF CIRCUIT 20	24	2		
2	25	PART OF CIRCUIT 23	-	1.9	0.2			1P20A	R - RADON EXHAUST FAN	26	2			
2	27	PART OF CIRCUIT 23	-		1.9	0.8		1P20A	L - A101	28	2			
2	29	R - RADON EXHAUST FAN	1P20A				0.2	0.2	1P20A	HT-A1/A2 CONTROL PANEL	30	2		
38	31	MAF-A1	3P100A	7.2	0.0			1P20A	SPARE	32	2			
38	33	PART OF CIRCUIT 31	-		7.2	0.0		1P20A	SPARE	34	2			
38	35	PART OF CIRCUIT 31	-				7.2	0.0	1P20A	SPARE	36	2		
38	37	PANEL 2A4A	3P100A	2.5	0.0			3P30A	SURGE PROTECTIVE DEVICE	38	5.5			
38	39	PART OF CIRCUIT 37	-		2.5	0.0		-	PART OF CIRCUIT 38	40	5.5			
38	41	PART OF CIRCUIT 37	-				2.5	0.0	-	PART OF CIRCUIT 38	42	5.5		
(linked from other panel)				0.0	0.0	0.0								
TOTAL PHASE A, B, C				20.3	21.3	20.0	NOTES:							
CONNECTED KVA:				61.6	KVA									
DEMAND FACTOR:				99	%									
DEMAND KVA:				61.0	KVA									
DEMAND AMPS:				169	AMPS									
DEMAND KVA				A	B	C								
				20.2	21.1	19.7								

[illegible]

 USAED-J, UNIT 35132 APO, AF 96374-5132	 SSF INTERNATIONAL, INC 501 SUMNER STREET, SUITE 620 HONOLULU, HAWAII 96817	CHECKED BY: _____ SUBMITTED BY: _____ SCALE: AS SHOWN	OCCASION NO.: _____ FILE NAME: _____ ISO A1
---	--	---	---

FY20 MCA PN77833

SHEET ID
E-712

[illegible][illegible]

	31	PFB			0.0	0.0		
	33	PFB					0.0	0.0
	35	PFB						
	37	SPARE	1P20A	0.0	0.0		0.0	0.0
	39	SPARE	1P20A			0.0	0.0	
	41	SPARE	1P20A				0.0	0.0
(linked from other panel)				0.0		0.0		0.0
TOTAL PHASE A, B, C				5.0		4.9		5.1
CONNECTED KVA:				15.0		KVA		
DEMAND FACTOR:				97		%		
DEMAND KVA:				14.5		KVA		
DEMAND AMPS:				40		AMPS		
DEMAND KVA				A		B		C
				4.9		4.8		4.8

PANEL: "2AT1"			VOLTAGE: 208Y/120V			3 PHASE		
MAIN BUS: 100A			MAIN BKR: 3P100A			4 WIRE		
MOUNTING: SURFACE			BKR TYPE: BOLT-ON					
WIRE	CKT NO.	DESCRIPTION	CKT BKR	KVA				
				A		B		C
2	1	R - TR	1P20A	0.5	0.5			
2	3	R - TR	1P20A			0.4	1.0	
2	5	R - TELECOM CABINET	2P20A					1.0
2	7	PART OF CIRCUIT 5	-	1.0	1.0			
2	9	R - TELECOM CABINET	1P20A			1.0	0.4	
	11	PFB						0.0
								0.4

	31	PFB			0.0	0.0		
	33	PFB					0.0	0.0
	35	PFB						
	37	SPARE	1P20A	0.0	0.0		0.0	0.0
	39	SPARE	1P20A			0.0	0.0	
	41	SPARE	1P20A				0.0	0.0
(linked from other panel)				0.0		0.0		0.0
TOTAL PHASE A, B, C				5.0		4.9		5.1
CONNECTED KVA:				15.0		KVA		
DEMAND FACTOR:				97		%		
DEMAND KVA:				14.5		KVA		
DEMAND AMPS:				40		AMPS		
DEMAND KVA				A		B		C
				4.9		4.8		4.8

[illegible]

		CONTRACT NO.:	
USAED-J, UNIT 35132 APO, AP 96374-5132		CHECKED BY:	
S5PM INTERNATIONAL, INC. 501 SUMNER STREET, SUITE 620 HONOLULU, HAWAII 96817		SUBMITTED BY:	
SIZE:		SCALE: AS SHOWN	
ISO A1		FILE NAME:	

FY20 MCA PN77833
 PANEL SCHEDULES

SHEET ID
E-713

PANEL: "2AELV"			VOLTAGE: 208Y/120V		3 PHASE		POLES: 42						
MAIN BUS: 100A			MAIN BKR: 3P100A		4 WIRE		MIN. A.I.C.: 65,000						
MOUNTING: SURFACE			BKR TYPE: BOLT-ON				CABINET WIDTH: 20"						
WIRE	CKT NO.	DESCRIPTION	CKT BKR	KVA			CKT BKR	DESCRIPTION	CKT NO.	WIRE			
				A	B	C							
2	1	R - ELEV EQUIPMENT ROOM	1P20A	0.4	3.7			3P60A	ELEVATOR	2	14		
2	3	R - ELEV PIT	1P20A			0.2	3.7	-	PART OF CIRCUIT 2	4	14		
2	5	R/L - ELEV CAB	1P20A					0.4	3.7	-	PART OF CIRCUIT 2	6	14
2	7	L - ELEV EQUIPMENT ROOM	1P20A	0.2	0.7					2P20A	ACCU-A6	8	2
2	9	L - ELEV PIT, HOISTWAT	1P20A			0.9	0.7			-	PART OF CIRCUIT 8	10	2
2	11	SP-A1	3P15A					0.3	0.0		PFB	12	
2	13	PART OF CIRCUIT 11	-	0.3	0.0						PFB	14	
2	15	PART OF CIRCUIT 11	-			0.3	0.0				PFB	16	
2	17	SP CONTROLLER	1P20A					0.2	0.0		PFB	18	
	19	PFB		0.0	0.0						PFB	20	
	21	PFB				0.0	0.0				PFB	22	
	23	PFB						0.0	0.0		PFB	24	
	25	PFB		0.0	0.0						PFB	26	
	27	PFB				0.0	0.0				PFB	28	
	29	PFB						0.0	0.0		PFB	30	
	31	PFB		0.0	0.0					1P20A	SPARE	32	
	33	PFB				0.0	0.0			1P20A	SPARE	34	
	35	PFB						0.0	0.0	1P20A	SPARE	36	
	37	SPARE	1P20A	0.0	0.0					3P30A	SURGE PROTECTIVE DEVICE	38	5.5
	39	SPARE	1P20A			0.0	0.0			-	PART OF CIRCUIT 38	40	5.5
	41	SPARE	1P20A					0.0	0.0	-	PART OF CIRCUIT 38	42	5.5
(linked from other panel)				0.0	0.0	0.0							
TOTAL PHASE A, B, C				5.2	5.8	4.5	<u>NOTES:</u>						
CONNECTED KVA:				15.6	KVA								
DEMAND FACTOR:				99	%								
DEMAND KVA:				15.3	KVA								
DEMAND AMPS:				43	AMPS								
DEMAND KVA				A	B	C							
				5.2	5.7	4.5							

PANEL: "28"				VOLTAGE: 208Y/120V			3 PHASE			POLES: 42		
MAIN BUS: 100A				MAIN BKR: 3P100A			4 WIRE			MIN. A.I.C.: 65,000		
MOUNTING: SURFACE				BKR TYPE: BOLT-ON						CABINET WIDTH: 20"		
WIRE	CKT NO.	DESCRIPTION	CKT BKR	KVA			CKT BKR	DESCRIPTION	CKT NO.	WIRE		
				A	B	C						
2	1	R - HQ STORAGE	1P20A	0.4	0.5			1P20A	L - HQ STORAGE	2	2	
2	3	R - ECHO STORAGE	1P20A		0.4	0.5		1P20A	L - ECHO STORAGE	4	2	
2	5	R - DELTA STORAGE	1P20A				0.4	0.5	1P20A	L - DELTA STORAGE	6	2
2	7	R - CHARLIE STORAGE	1P20A	0.4	0.5			1P20A	L - CHARLIE STORAGE	8	2	
2	9	R - BRAVO STORAGE	1P20A		0.4	0.5		1P20A	L - BRAVO STORAGE	10	2	
2	11	R - ALPHA STORAGE	1P20A				0.4	0.5	1P20A	L - ALPHA STORAGE	12	2
2	13	EF-B5,EF-B6	2P15A	0.8	1.0			2P20A	ACCU-B5,ACCU-B6,FCU-B5,FCU-B6	14	2	
2	15	PART OF CIRCUIT 13	-		0.8	1.0		-	PART OF CIRCUIT 14	16	2	
2	17	EF-B3,EF-B4	2P15A				0.8	1.0	2P20A	ACCU-B3,ACCU-B4,FCU-B3,FCU-B4	18	2
2	19	PART OF CIRCUIT 17	-	0.8	1.0			-	PART OF CIRCUIT 18	20	2	
2	21	EF-B1,EF-B2	2P15A		0.8	1.0		2P20A	ACCU-B1,ACCU-B2,FCU-B1,FCU-B2	22	2	
2	23	PART OF CIRCUIT 21	-				0.8	1.0	-	PART OF CIRCUIT 22	24	2
2	25	R - EXTERIOR	1P20A	0.5	1.0			2P20A	L - PARKING	26	5.5	
2	27	LIGHTING INVERTER	1P20A		1.0	1.0		-	PART OF CIRCUIT 26	28	5.5	
	29	PFB					0.0	0.0	PFB		30	
	31	PFB		0.0	0.0				PFB		32	
	33	PFB			0.0	0.0			PFB		34	
	35	PFB					0.0	0.0	PFB		36	
	37	SPARE	1P20A	0.0	0.0			3P30A	SURGE PROTECTIVE DEVICE	38	5.5	
	39	SPARE	1P20A		0.0	0.0		-	PART OF CIRCUIT 38	40	5.5	
	41	SPARE	1P20A				0.0	0.0	-	PART OF CIRCUIT 38	42	5.5
(linked from other panel)				0.0	0.0	0.0						
TOTAL PHASE A, B, C				6.8	7.2	5.2	<u>NOTES:</u>					
CONNECTED KVA:				19.2	KVA							
DEMAND FACTOR:				99	%							
DEMAND KVA:				18.9	KVA							
DEMAND AMPS:				53	AMPS							
DEMAND KVA				A	B	C						
				6.7	7.1	5.1						

PANEL: "2C"			VOLTAGE: 208Y/120V			3 PHASE			POLES: 42		
MAIN BUS: 100A			MAIN BKR: 3P100A			4 WIRE			MIN. A.I.C.: 65,000		
MOUNTING: SURFACE			BKR TYPE: BOLT-ON						CABINET WIDTH: 20"		
WIRE	CKT NO.	DESCRIPTION	CKT BKR	KVA		C	CKT BKR	DESCRIPTION	CKT NO.	WIRE	
				A	B						
2	1	R - STORAGE	1P20A	0.5	0.5		1P20A	L - UTILITY	2	2	
2	3	R - STORAGE	1P20A		0.4	0.8		2P15A	EF-C1,EF-C2	4	2
2	5	R - EYE WASH STATION	1P20A			1.0	0.8	-	PART OF CIRCUIT 4	6	2
2	7	R - EXTERIOR	1P20A	1.0	1.0			1P20A	LIGHTING INVERTER	8	2
	9	PFB			0.0	0.0		PFB		10	
	11	PFB				0.0	0.0	PFB		12	
	13	PFB		0.0	0.0			PFB		14	
	15	PFB			0.0	0.0		PFB		16	
	17	PFB				0.0	0.0	PFB		18	
	19	PFB		0.0	0.0			PFB		20	
	21	PFB			0.0	0.0		PFB		22	
	23	PFB				0.0	0.0	PFB		24	
	25	PFB		0.0	0.0			PFB		26	
	27	PFB			0.0	0.0		PFB		28	
	29	PFB				0.0	0.0	PFB		30	
	31	PFB		0.0	0.0			1P20A	SPARE	32	
	33	PFB			0.0	0.0		1P20A	SPARE	34	
	35	PFB				0.0	0.0	1P20A	SPARE	36	
	37	SPARE	1P20A	0.0	0.0			3P30A	SURGE PROTECTIVE DEVICE	38	5.5
	39	SPARE	1P20A		0.0	0.0		-	PART OF CIRCUIT 38	40	5.5
	41	SPARE	1P20A			0.0	0.0	-	PART OF CIRCUIT 38	42	5.5
(linked from other panel)				0.0	0.0	0.0					
TOTAL PHASE A, B, C				3.0	1.2	1.8	<u>NOTES:</u>				
CONNECTED KVA:				6.1	KVA						
DEMAND FACTOR:				92	%						
DEMAND KVA:				5.6	KVA						
DEMAND AMPS:				16	AMPS						
DEMAND KVA				A	B	C					
				2.9	1.1	1.6					

E-714

PANEL: "2D3"			VOLTAGE: 208Y/120V			3 PHASE		POLES: 42				
MAIN BUS: 100A			MAIN BKR: 3P100A			4 WIRE		MIN. A.I.C.: 65,000				
MOUNTING: SURFACE			BKR TYPE: BOLT-ON					CABINET WIDTH: 20"				
WIRE	CKT NO.	DESCRIPTION	CKT BKR	KVA			CKT BKR	DESCRIPTION	CKT NO.	WIRE		
				A	B	C						
2	1	R - WAREHOUSE	1P20A	0.2	1.3		3P20A	EF-D6.3	2	2		
2	3	R - WAREHOUSE	1P20A		0.2	1.3	-	PART OF CIRCUIT 2	4	2		
2	5	HVLS-D2	3P15A				-	PART OF CIRCUIT 2	6	2		
2	7	PART OF CIRCUIT 5	-	0.8	0.7		0.8	1.3	1P20A	8	2	
2	9	PART OF CIRCUIT 5	-		0.8	0.7			1P20A	10	2	
2	11	ETP	1P15A				0.2	0.0	PFB	12		
	13	PFB		0.0	0.0				PFB	14		
	15	PFB			0.0	0.0			PFB	16		
	17	PFB					0.0	0.0	PFB	18		
	19	PFB		0.0	0.0				PFB	20		
	21	PFB			0.0	0.0			PFB	22		
	23	PFB					0.0	0.0	PFB	24		
	25	PFB		0.0	0.0				PFB	26		
	27	PFB			0.0	0.0			PFB	28		
	29	PFB					0.0	0.0	PFB	30		
	31	PFB		0.0	0.0				1P20A	32		
	33	PFB			0.0	0.0			1P20A	34		
	35	PFB					0.0	0.0	1P20A	36		
	37	SPARE	1P20A	0.0	0.0				3P30A	SURGE PROTECTIVE DEVICE	38	5.5
	39	SPARE	1P20A		0.0	0.0			-	PART OF CIRCUIT 38	40	5.5
	41	SPARE	1P20A				0.0	0.0	-	PART OF CIRCUIT 38	42	5.5
(linked from other panel)				0.0	0.0	0.0						
TOTAL PHASE A, B, C				3.0	3.0	2.3	NOTES:					
CONNECTED KVA:				8.3	KVA							
DEMAND FACTOR:				96	%							
DEMAND KVA:				8.0	KVA							
DEMAND AMPS:				22	AMPS							
DEMAND KVA				A	B	C						
				3.0	3.0	2.1						

[illegible]

USAED-J, UNIT 35132 APO, AP 96374-5132			SUBMITTED BY:	SCALE: AS SHOWN	CONSTRUCTION NO.:
	S50F INTERNATIONAL, INC. 501 SUMNER STREET, SUITE 620 HONOLULU, HAWAII 96817		CHECKED BY:	SIZE: ISO A1	FILE NAME:


FY20 MCA PN77833
PANEL SCHEDULES

SHEET ID
E-715

	32	
	34	
	36	
EVIC	38	5.5
	40	5.5
	42	5.5

			PANEL: "2G"	
			MAIN BUS: 100A	
			MOUNTING: SURFACE	
			WIRE	DESCRIPTION
			CTK NO.	
			2	1 R - UTILITY
			2	3 R - UTILITY
			6	5 R - TELECOM CABINET
			8	7 R - TELECOM CABINET
			10	9 R - TELECOM CABINET
			12	11 PART OF CIRCUIT 9
			14	13 R - EXTERIOR
			16	15 PFB
			18	17 PFB
			20	19 PFB
			22	21 PFB
			24	23 PFB
			26	25 PFB
			28	27 PFB
			30	29 PFB
			32	31 PFB

PANEL "2G"			VOLTAGE: 208Y/120V			3 PHASE			POLES: 42			
MAIN BUS: 100A			MAIN BKR: 3P100A			4 WIRE			MIN. A.I.C.: 65,000			
MOUNTING: SURFACE			BKR TYPE: BOLT-ON						CABINET WIDTH: 20"			
WIRE	CKT NO.	DESCRIPTION	CKT BKR	KVA			CKT BKR	DESCRIPTION	CKT NO.	WIRE		
				A	B	C						
2	1	R - UTILITY	1P20A	0.5	0.5			1P20A	L - UTILITY	2	2	
2	3	R - UTILITY	1P20A		0.4	1.0		1P20A	R - TELECOM CABINET	4	2	
2	5	R - TELECOM CABINET	2P20A				1.0	1.0	1P20A	PART OF CIRCUIT 4	6	2
2	7	R - TELECOM CABINET	-	1.0	0.5			2P15A	ACCU-G1,FCU-G1	8	2	
2	9	R - TELECOM CABINET	1P20A		1.0	0.5		-	PART OF CIRCUIT 8	10	2	
2	11	PART OF CIRCUIT 9	1P20A				1.0	0.0	PFB	12		
2	13	R - EXTERIOR	1P20A	0.2	0.0				PFB	14		
	15	PFB			0.0	0.0			PFB	16		
	17	PFB					0.0	0.0	PFB	18		
	19	PFB		0.0	0.0				PFB	20		
	21	PFB			0.0	0.0			PFB	22		
	23	PFB					0.0	0.0	PFB	24		
	25	PFB		0.0	0.0				PFB	26		
	27	PFB			0.0	0.0			PFB	28		
	29	PFB					0.0	0.0	PFB	30		
	31	PFB		0.0	0.0			1P20A	SPARE	32		
	33	PFB			0.0	0.0		1P20A	SPARE	34		
	35	PFB					0.0	0.0	1P20A	SPARE	36	
	37	SPARE	1P20A	0.0	0.0			3P30A	SURGE PROTECTIVE DEVICE	38	5.5	
	39	SPARE	1P20A		0.0	0.0		-	PART OF CIRCUIT 38	40	5.5	
	41	SPARE	1P20A				0.0	0.0	-	PART OF CIRCUIT 38	42	5.5
(linked from other panel)			0.0	0.0	0.0							
TOTAL PHASE A, B, C			2.7	2.9	3.0	NOTES:						
CONNECTED KVA:			8.6	KVA								
DEMAND FACTOR:			94	%								
DEMAND KVA:			8.1	KVA								
DEMAND AMPS:			22	AMPS								
DEMAND KVA			A	B	C							
			2.6	2.8	2.8							

 		SSMF INTERNATIONAL, INC. 507 SUMNER STREET, SUITE 620 HONOLULU, HAWAII 96817	
COUNTRY: USA-ED-J, UNIT 35132 APO, AP 96374-5132	CHECKED BY: 	SUBMITTED BY: 	SCALE: AS SHOWN
COLLECTION NO.: 	CONTRACT NO.: 	SIZE: ISO A1	FILE NAME:

SHEET ID
E-716

PANEL: "2H1"				VOLTAGE: 208Y/120V				3 PHASE		POLES:		42	
MAIN BUS: 100A				MAIN BKR: 3P100A				4 WIRE		MIN. A.I.C.:		65,000	
MOUNTING: SURFACE				BOLT-ON						CABINET WIDTH:		20"	
WIRE	CKT NO.	DESCRIPTION	CKT BKR	KVA						CKT BKR	DESCRIPTION	CKT NO.	WIRE
				A		B		C					
2	1	R - HALL, EXTERIOR	1P20A	0.7	0.9					1P20A	R - H210,H212	2	2
2	3	R - JAN, MEN, WOMEN	1P20A			0.9	0.7			1P20A	R - H216-H217	4	2
2	5	R - H230,H232	1P20A					0.9	0.5	1P20A/G	R - FRIDGE H212	6	2
2	7	R - H236-H237	1P20A	0.5	0.2					1P20A	R - COUNTERTOP H212	8	2
2	9	R - FRIDGE H232	1P20A/G			0.5	0.2			1P20A	R - COUNTERTOP H212	10	2
	11	PFB						0.4	0.7	1P20A	R - OFFICE H214-H215	12	2
2	13	R - H130,H132	1P20A	0.9	0.5					1P20A	R - OFFICE H213, RECEPTION H211	14	2
2	15	R - H136-H137	1P20A			0.7	0.9			1P20A	R - H220,H222	16	2
2	17	R - FRIDGE H132	1P20A/G					0.5	0.7	1P20A	R - H226-H227	18	2
2	19	R - COUNTERTOP H132	1P20A	0.2	0.5					1P20A/G	R - FRIDGE H222	20	2
2	21	R - COUNTERTOP H132	1P20A			0.2	0.2			1P20A	R - COUNTERTOP H222	22	2
2	23	R - OFFICE H134-H135	1P20A					0.7	0.2	1P20A	R - COUNTERTOP H222	24	2
2	25	R - OFFICE H133, RECEPTION H131	1P20A	0.5	0.7					1P20A	R - OFFICE H224-H225	26	2
2	27	R - COUNTERTOP H232	1P20A			0.0	0.5			1P20A	R - OFFICE H223, RECEPTION H221	28	2
2	29	R - COUNTERTOP H232	1P20A					0.0	0.7	1P20A	R - OFFICE H234-H235	30	2
	31	SPARE	1P20A	0.0	0.5					1P20A	R - OFFICE H233, RECEPTION H231	32	2
	33	SPARE	1P20A			0.0	1.0			1P20A	LIGHTING INVERTER	34	2
	35	SPARE	1P20A					0.0	0.0		PFB	36	
	37	SPARE	1P20A	0.0	0.0					3P30A	SURGE PROTECTIVE DEVICE	38	5.5
	39	SPARE	1P20A			0.0	0.0			-	PART OF CIRCUIT 38	40	5.5
	41	SPARE	1P20A					0.0	0.0	-	PART OF CIRCUIT 38	42	5.5
(linked from other panel)				0.0		0.0		0.0					
TOTAL PHASE A, B, C				6.3		5.9		5.3	NOTES:				
CONNECTED KVA:				17.4		KVA							
DEMAND FACTOR:				96		%							
DEMAND KVA:				16.8		KVA							
DEMAND AMPS:				47		AMPS							
DEMAND KVA				A		B		C					
				6.1		5.6		5.1					

PANEL: "2HT1"			VOLTAGE: 208Y/120V			3 PHASE			POLES: 42		
MAIN BUS: 100A			MAIN BKR: 3P100A			4 WIRE			MIN. A.I.C.: 65,000		
MOUNTING: SURFACE			BKR TYPE: BOLT-ON						CABINET WIDTH: 20"		
WIRE	CKT NO.	DESCRIPTION	CKT BKR	KVA			CKT BKR	DESCRIPTION	CKT NO.	WIRE	
				A	B	C					
2	1	R - TR	1P20A	0.5	0.5		1P20A	R - TR	2	2	
2	3	R - TR	1P20A		0.4	1.0	2P20A	R - TELECOM CABINET	4	2	
2	5	R - TELECOM CABINET	2P20A				-	PART OF CIRCUIT 4	6	2	
2	7	PART OF CIRCUIT 5	-	1.0	1.0		1P20A	R - TELECOM CABINET	8	2	
2	9	R - TELECOM CABINET	1P20A		1.0	0.0		PFB		10	
	11	PFB					0.0	0.0		12	
	13	PFB		0.0	0.0					14	
	15	PFB			0.0	0.0				16	
	17	PFB				0.0	0.0			18	
	19	PFB		0.0	0.0					20	
	21	PFB			0.0	0.0				22	
	23	PFB				0.0	0.0			24	
	25	PFB		0.0	0.0					26	
	27	PFB			0.0	0.0				28	
	29	PFB				0.0	0.0			30	
	31	PFB		0.0			1P20A	SPARE		32	
	33	PFB			0.0	0.0	1P20A	SPARE		34	
	35	PFB				0.0	0.0	1P20A	SPARE	36	
	37	SPARE	1P20A	0.0	0.0		3P30A	SURGE PROTECTIVE DEVICE	38	5.5	
	39	SPARE	1P20A		0.0	0.0	-	PART OF CIRCUIT 38	40	5.5	
	41	SPARE	1P20A			0.0	0.0	-	PART OF CIRCUIT 38	42	5.5
(linked from other panel)				0.0	0.0	0.0					
TOTAL PHASE A, B, C				3.0	2.4	2.0	NOTES:				
CONNECTED KVA:				7.4	KVA						
DEMAND FACTOR:				94	%						
DEMAND KVA:				6.9	KVA						
DEMAND AMPS:				19	AMPS						
DEMAND KVA				A	B	C					
				2.9	2.3	1.8					

[illegible]

USAED-J, UNIT 35132 APO, AP 96374-5132			SUBMITTED BY:	SCALE: AS SHOWN	CONSTRUCTION NO.:
	S50F INTERNATIONAL, INC. 501 SUMNER STREET, SUITE 620 HONOLULU, HAWAII 96817		CHECKED BY:	SIZE: ISO A1	FILE NAME:

FY20 MCA PN77833
PANEL SCHEDULES

SHEET ID
E-717

PANEL: "120H"			VOLTAGE: 208Y/120V			3 PHASE			POLES: 42				
MAIN BUS: 100A			MAIN BKR: 3P100A			4 WIRE			MIN. A.I.C.: 65,000				
MOUNTING: SURFACE			BKR TYPE: 20T-ON						CABINET WIDTH: 20"				
WIRE	CKT NO.	DESCRIPTION	CKT BKR	KVA			CKT BKR	DESCRIPTION	CKT NO.	WIRE			
				A	B	C							
2	1	R - MECH YARD	1P20A	0.4	1.0			2P20A	ACCU-H1	2	2		
2	3	EF VIA STEP DOWN XFMR	1P15A			0.2	1.0	-	PART OF CIRCUIT 2	4	2		
2	5	EF VIA STEP DOWN XFMR	1P15A					0.2	1.2	2P20A	ACCU-H2	6	2
2	7	PFB		0.0	1.2					-	PART OF CIRCUIT 6	8	2
2	9	ACCU-H7	2P20A			1.0	0.6			2P20A	ACCU-H3	10	2
2	11	PART OF CIRCUIT 9	-					1.0	0.6	-	PART OF CIRCUIT 10	12	2
2	13	ACCU-H8	2P20A	0.9	0.9					2P20A	ACCU-H4	14	2
2	15	PART OF CIRCUIT 13	-			0.9	0.9			-	PART OF CIRCUIT 14	16	2
2	17	ACCU-H9	2P20A					0.9	0.9	2P20A	ACCU-H5	18	2
2	19	PART OF CIRCUIT 17	-	0.9	0.9					-	PART OF CIRCUIT 18	20	2
2	21	ACCU-H10	2P20A			1.2	1.2			2P20A	ACCU-H6	22	2
2	23	PART OF CIRCUIT 21	-					1.2	1.2	-	PART OF CIRCUIT 22	24	2
2	25	ACCU-H11	2P20A	0.9	0.4					1P20A	R - RADON EXHAUST FAN	26	2
2	27	PART OF CIRCUIT 25	-			0.9	0.4			1P20A	R - RADON EXHAUST FAN	28	2
2	29	ACCU-H12	2P20A					1.2	0.5	1P20A	R - RADON EXHAUST FAN	30	2
2	31	PART OF CIRCUIT 29	-	1.2	0.0					1P20A	SPARE	32	
	33	PFB				0.0	0.0			1P20A	SPARE	34	
	35	PFB						0.0	0.0	1P20A	SPARE	36	
	37	SPARE	1P20A	0.0	0.0					3P30A	SURGE PROTECTIVE DEVICE	38	5.5
	39	SPARE	1P20A			0.0	0.0			-	PART OF CIRCUIT 38	40	5.5
	41	SPARE	1P20A			0.0	0.0	0.0	0.0	-	PART OF CIRCUIT 38	42	5.5
(linked from other panel)				0.0	0.0	0.0							
TOTAL PHASE A, B, C				8.6	8.2	8.9	<u>NOTES:</u>						
CONNECTED KVA:				25.8	KVA								
DEMAND FACTOR:				99	%								
DEMAND KVA:				25.6	KVA								
DEMAND AMPS:				71	AMPS								
DEMAND KVA				A	B	C							
				8.5	8.2	8.9							

PANEL: "2WR"			VOLTAGE: 208Y/120V			3 PHASE			POLES: 42				
MAIN BUS: 400A			MAIN BKR: 3P400A			4 WIRE			MIN. A.I.C.: 65,000				
MOUNTING: SURFACE			BKR TYPE: BOLT-ON						CABINET WIDTH: 20"				
WIRE	CKT NO.	DESCRIPTION	CKT BKR	KVA			CKT BKR	DESCRIPTION	CKT NO.	WIRE			
				A	B	C							
8	1	WWRS-11	3P40A	4.0	3.0			3P30A	PW-11	2	5.5		
8	3	PART OF CIRCUIT 1	-			4.0	3.0	-	PART OF CIRCUIT 2	4	5.5		
8	5	PART OF CIRCUIT 1	-					4.0	3.0	-	PART OF CIRCUIT 2	6	5.5
8	7	WWRS-12	3P40A	4.0	3.0					3P30A	PW-12	8	5.5
8	9	PART OF CIRCUIT 7	-			4.0	3.0	-	PART OF CIRCUIT 8	10	5.5		
8	11	PART OF CIRCUIT 7	-					4.0	3.0	-	PART OF CIRCUIT 8	12	5.5
8	13	WWRS-13	3P40A	4.0	3.0					3P30A	PW-13	14	5.5
8	15	PART OF CIRCUIT 13	-			4.0	3.0	-	PART OF CIRCUIT 14	16	5.5		
8	17	PART OF CIRCUIT 13	-					4.0	3.0	-	PART OF CIRCUIT 14	18	5.5
5.5	19	L - PARKING	2P20A	1.0	1.0					2P20A	L - PARKING	20	5.5
5.5	21	PART OF CIRCUIT 19	-			1.0	1.0	-	PART OF CIRCUIT 20	22	5.5		
	23	PFB						0.0	0.0		PFB	24	
	25	PFB		0.0	0.0						PFB	26	
	27	PFB				0.0	0.0				PFB	28	
	29	PFB						0.0	0.0		PFB	30	
	31	PFB		0.0	0.0						PFB	32	
	33	PFB				0.0	0.0				PFB	34	
	35	PFB						0.0	0.0		PFB	36	
	37	SPARE	1P20A	0.0	0.0					3P30A	SURGE PROTECTIVE DEVICE	38	5.5
	39	SPARE	1P20A			0.0	0.0	-	PART OF CIRCUIT 38	40	5.5		
	41	SPARE	1P20A					0.0	0.0	-	PART OF CIRCUIT 38	42	5.5
(linked from other panel)				0.0	0.0	0.0							
TOTAL PHASE A, B, C				23.0	23.0	21.0	<u>NOTES:</u>						
CONNECTED KVA:				67.0	KVA								
DEMAND FACTOR:				100	%								
DEMAND KVA:				67.0	KVA								
DEMAND AMPS:				186	AMPS								
DEMAND KVA				A	B	C							
				23.0	23.0	21.0							

PANEL: "2E"			VOLTAGE: 208Y/120V			3 PHASE			POLES: 42			
MAIN BUS: 100A			MAIN BKR: 3P100A			4 WIRE			MIN. A.I.C.: 65,000			
MOUNTING: SURFACE			BKR TYPE: BOLT-ON						CABINET WIDTH: 20"			
WIRE	CKT NO.	DESCRIPTION	CKT BKR	KVA					CKT BKR	DESCRIPTION	CKT NO.	WIRE
				A	B	C						
2	1	R - STORAGE SHED	1P20A	0.5	0.9				1P20A	L - STORAGE SHED	2	2
2	3	R - STORAGE SHED	1P20A		0.5	0.9			1P20A	L - STORAGE SHED	4	2
2	5	R - STORAGE SHED	1P20A				0.5	0.3	2P15A	EF-F1	6	2
	7	PFB		0.0	0.3				-	PART OF CIRCUIT 6	8	2
	9	PFB			0.0	0.0				PFB		10
	11	PFB					0.0	0.0		PFB		12
	13	PFB		0.0	0.0					PFB		14
	15	PFB			0.0	0.0				PFB		16
	17	PFB					0.0	0.0		PFB		18
	19	PFB		0.0	0.0					PFB		20
	21	PFB			0.0	0.0				PFB		22
	23	PFB					0.0	0.0		PFB		24
	25	PFB		0.0	0.0					PFB		26
	27	PFB			0.0	0.0				PFB		28
	29	PFB					0.0	0.0	-	PFB		30
	31	PFB		0.0	0.0				1P20A	SPARE		32
	33	PFB			0.0	0.0			1P20A	SPARE		34
	35	PFB					0.0	0.0	1P20A	SPARE		36
	37	SPARE	1P20A	0.0	0.0				3P30A	SURGE PROTECTIVE DEVICE	38	5.5
	39	SPARE	1P20A		0.0	0.0			-	PART OF CIRCUIT 38	40	5.5
	41	SPARE	1P20A				0.0	0.0	-	PART OF CIRCUIT 38	42	5.5
(linked from other panel)				0.0	0.0	0.0						
TOTAL PHASE A, B, C				1.7	1.4	0.8	NOTES:					
CONNECTED KVA:				3.9	KVA							
DEMAND FACTOR:				90	%							
DEMAND KVA:				3.5	KVA							
DEMAND AMPS:				10	AMPS							
DEMAND KVA				A	B	C						
				1.6	1.3	0.7						

[illegible]



USAED-J, UNIT 35132 APO, AP 96374-5132	 SSM INTERNATIONAL, INC. 501 SUFFERN STREET, SUITE 620 HONOLULU, HAWAII 96817	CHECKED BY:	CONTRACT NO.:
		SUBMITTED BY:	SCALE: AS SHOWN
		SIZE:	FILE NAME:
		ISO A1	

FY20 MICA PN77833
PANEL SCHEDULES





SHEET ID
E-718

PANEL: "2A3A"			VOLTAGE: 208Y/120V			3 PHASE			POLES: 42		
MAIN BUS: 100A			MAIN BKR: 3P100A			4 WIRE			MIN. A.I.C.: 65,000		
MOUNTING: SURFACE			BKR TYPE: BOLT-ON						CABINET WIDTH: 20"		
WIRE	CKT NO.	DESCRIPTION	CKT BKR	KVA			CKT BKR	DESCRIPTION	CKT NO.	WIRE	
				A	B	C					
2	1	EF-A1.5	3P15A	0.5	0.5		3P15A	EF-A1.7	2	2	
2	3	PART OF CIRCUIT 1	-		0.5	0.5	-	PART OF CIRCUIT 2	4	2	
2	5	PART OF CIRCUIT 1	-			0.5	0.5	PART OF CIRCUIT 2	6	2	
2	7	EF-A1.6	3P15A	0.5	0.2		1P15A	ETP	8	2	
2	9	PART OF CIRCUIT 7	-		0.5	0.0		PFB	10		
2	11	PART OF CIRCUIT 7	-			0.5	0.0	PFB	12		
	13	PFB		0.0	0.0			PFB	14		
	15	PFB			0.0	0.0		PFB	16		
	17	PFB				0.0	0.0	PFB	18		
	19	PFB		0.0	0.0			PFB	20		
	21	PFB			0.0	0.0		PFB	22		
	23	PFB				0.0	0.0	PFB	24		
	25	PFB		0.0	0.0			PFB	26		
	27	PFB			0.0	0.0		PFB	28		
	29	PFB				0.0	0.0	PFB	30		
	31	PFB		0.0	0.0		1P20A	SPARE	32		
	33	PFB			0.0	0.0	1P20A	SPARE	34		
	35	PFB				0.0	0.0	1P20A	SPARE	36	
	37	SPARE	1P20A	0.0	0.0		3P30A	SURGE PROTECTIVE DEVICE	38	5.5	
	39	SPARE	1P20A		0.0	0.0	-	PART OF CIRCUIT 38	40	5.5	
	41	SPARE	1P20A			0.0	0.0	-	PART OF CIRCUIT 38	42	5.5
(linked from other panel)				0.0	0.0	0.0					
TOTAL PHASE A, B, C				1.7	1.5	1.5	NOTES:				
CONNECTED KVA:				4.7	KVA						
DEMAND FACTOR:				92	%						
DEMAND KVA:				4.3	KVA						
DEMAND AMPS:				12	AMPS						
DEMAND KVA				A	B	C					
				1.6	1.4	1.4					

PANEL: "2A4A"			VOLTAGE: 208Y/120V			3 PHASE			POLES: 42			
MAIN BUS: 100A			MAIN BKR: 3P100A			4 WIRE			MIN. A.I.C.: 65,000			
MOUNTING: SURFACE			BKR TYPE: BOLT-ON						CABINET WIDTH: 20"			
WIRE	CKT NO.	DESCRIPTION	CKT BKR	KVA			CKT BKR	DESCRIPTION	CKT NO.	WIRE		
				A	B	C						
2	1	EF-A1.8	3P15A	0.5	0.5		3P15A	EF-A1.11	2	2		
2	3	PART OF CIRCUIT 1	-		0.5	0.5	-	PART OF CIRCUIT 2	4	2		
2	5	PART OF CIRCUIT 1	-				0.5	0.5	-	PART OF CIRCUIT 2	6	2
2	7	EF-A1.9	3P15A	0.5	0.5		3P15A	EF-A1.12	8	2		
2	9	PART OF CIRCUIT 7	-		0.5	0.5	-	PART OF CIRCUIT 8	10	2		
2	11	PART OF CIRCUIT 7	-				0.5	0.5	-	PART OF CIRCUIT 8	12	2
2	13	EF-A1.10	3P15A	0.5	0.2		1P15A	ETP	14	2		
2	15	PART OF CIRCUIT 13	-		0.5	0.0		PFB	16			
2	17	PART OF CIRCUIT 13	-				0.5	0.0	PFB	18		
2	19	EF-A1.11	3P15A	0.5	0.0			PFB	20			
2	21	PART OF CIRCUIT 19	-		0.5	0.0		PFB	22			
2	23	PART OF CIRCUIT 19	-				0.5	0.0	PFB	24		
	25	PFB		0.0	0.0			PFB	26			
	27	PFB			0.0	0.0		PFB	28			
	29	PFB					0.0	0.0	PFB	30		
	31	PFB		0.0	0.0		1P15A	SPARE	32			
	33	PFB			0.0	0.0	1P20A	SPARE	34			
	35	PFB					0.0	0.0	1P20A	SPARE	36	
	37	SPARE	1P20A	0.0	0.0		3P30A	SURGE PROTECTIVE DEVICE	38	5.5		
	39	SPARE	1P20A		0.0	0.0	-	PART OF CIRCUIT 38	40	5.5		
	41	SPARE	1P20A				0.0	0.0	-	PART OF CIRCUIT 38	42	5.5
(linked from other panel)				0.0	0.0	0.0						
TOTAL PHASE A, B, C				3.2	3.0	3.0	NOTES:					
CONNECTED KVA:				9.2	KVA							
DEMAND FACTOR:				96	%							
DEMAND KVA:				8.8	KVA							
DEMAND AMPS:				24	AMPS							
DEMAND KVA				A	B	C						
				3.1	2.9	2.9						

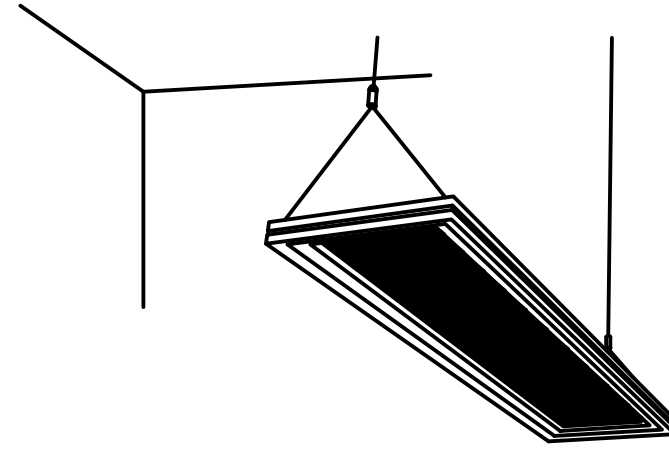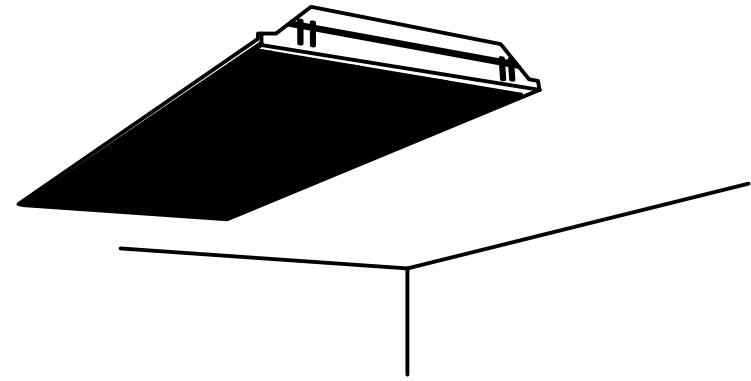

TYPE	LAMP & WATTS	MOUNTING	DESCRIPTION	
A	36W LED	RECESSED	600 X 1200, 3500K, MINIMUM 80 CRI UON, HIGH-EFFICIENCY DIMMABLE DRIVER, UNIVERSAL VOLTAGE, UL LISTED FOR DRY OR DAMP LOCATION, RECESSED IN HARD OR ACOUSTICAL TILE CEILING.	B	43W LED	PENDANT	300 X 1200 DIRECT/INDIRECT, 3500K, MINIMUM 80 CRI UON, HIGH-EFFICIENCY DIMMABLE DRIVER, UNIVERSAL VOLTAGE, UL LISTED FOR DRY OR DAMP LOCATION, PENDANT OR STEM MOUNTED WITH STAINLESS STEEL MOUNTING HARDWARE.	C	SURFACE	SURFACE	300 X 1200 WRAPAROUND, 3500K, MINIMUM 80 CRI UON, HIGH-EFFICIENCY DIMMABLE DRIVER, UNIVERSAL VOLTAGE, UL LISTED FOR DRY OR DAMP LOCATION, SURFACE MOUNTED.	D	63W LED	SURFACE	300 X 1200 WRAPAROUND, 3500K, MINIMUM 80 CRI UON, HIGH-EFFICIENCY DIMMABLE DRIVER, UNIVERSAL VOLTAGE, UL LISTED FOR DRY OR DAMP LOCATION, SURFACE MOUNTED.

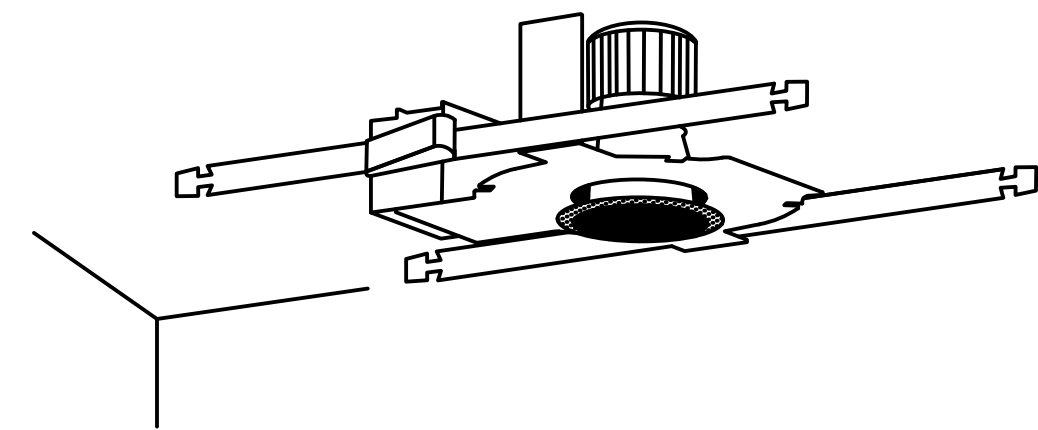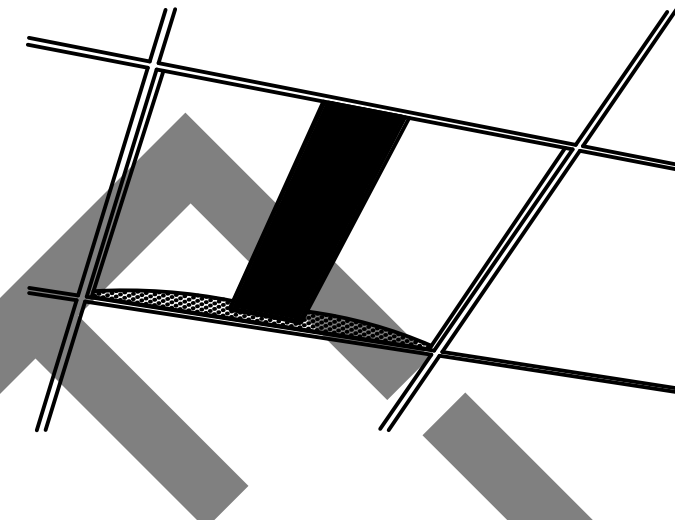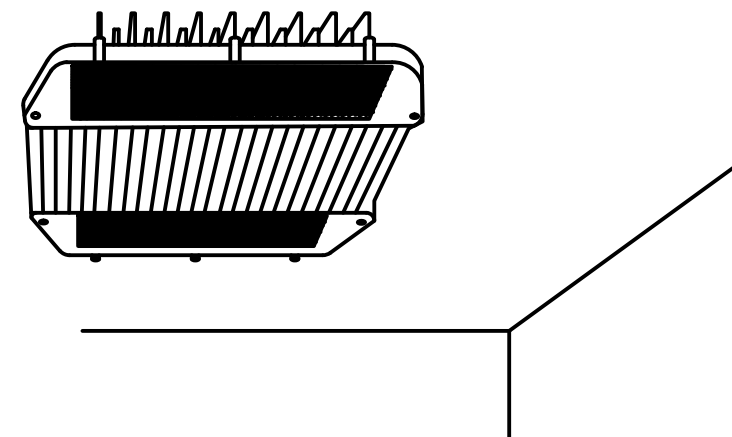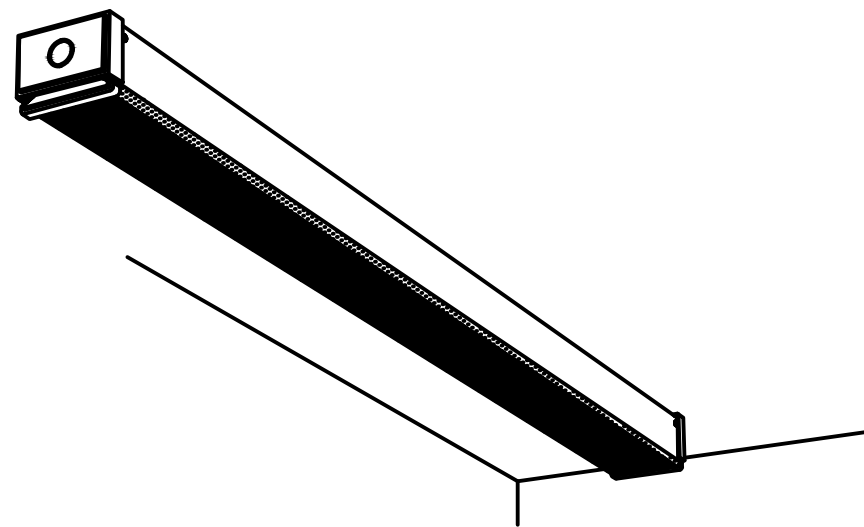

TYPE	LAMP & WATTS	MOUNTING	DESCRIPTION	
	55W LED	SURFACE	1200L, 3500K, MINIMUM 80 CRI UON, HIGH-EFFICIENCY DIMMABLE DRIVER, UNIVERSAL VOLTAGE, UL LISTED FOR DAMP OR WET LOCATION, SURFACE MOUNTED.		90W LED	SURFACE	HIGH-BAY, 3500K, MINIMUM 80 CRI UON, HIGH-EFFICIENCY DIMMABLE DRIVER, UNIVERSAL VOLTAGE, UL LISTED FOR DAMP OR WET LOCATION, PENDANT, STEM, OR SURFACE MOUNTED WITH STAINLESS STEEL MOUNTING HARDWARE.		50W LED	RECESSED	600 X 600, 3500K, MINIMUM 80 CRI UON, HIGH-EFFICIENCY DIMMABLE DRIVER, UNIVERSAL VOLTAGE, UL LISTED FOR DRY OR DAMP LOCATION, RECESSED IN HARD OR ACOUSTICAL TILE CEILING.		27W LED	RECESSED	FIXED RECESSED DOWNLIGHT, 3500K, MINIMUM 80 CRI UON, HIGH-EFFICIENCY DIMMABLE DRIVER, UNIVERSAL VOLTAGE, UL LISTED FOR DRY OR DAMP LOCATION, RECESSED IN HARD OR ACOUSTICAL TILE CEILING. PROVIDE T-BAR HANGERS FOR INSTALLATION IN ACOUSTICAL TILE CEILINGS OR TABS WHEN MOUNTING IN HARD CEILINGS.
				TYPE	LAMP & WATTS	MOUNTING	DESCRIPTION								
					64W LED	SURFACE	HIGH-BAY, 3500K, MINIMUM 80 CRI UON, HIGH-EFFICIENCY DIMMABLE DRIVER, UNIVERSAL VOLTAGE, UL LISTED FOR DAMP OR WET LOCATION, PENDANT, STEM, OR SURFACE MOUNTED WITH STAINLESS STEEL MOUNTING HARDWARE.								
				TYPE	LAMP & WATTS	MOUNTING	DESCRIPTION								
					178W LED	SURFACE	HIGH-BAY, 3500K, MINIMUM 80 CRI UON, HIGH-EFFICIENCY DIMMABLE DRIVER, UNIVERSAL VOLTAGE, UL LISTED FOR DAMP OR WET LOCATION, PENDANT, STEM, OR SURFACE MOUNTED WITH STAINLESS STEEL MOUNTING HARDWARE.								
					32W LED	RECESSED	600 X 600, 3500K, MINIMUM 80 CRI UON, HIGH-EFFICIENCY DIMMABLE DRIVER, UNIVERSAL VOLTAGE, UL LISTED FOR DRY OR DAMP LOCATION, RECESSED IN HARD OR ACOUSTICAL TILE CEILING.								



US Army Corps
of Engineers®

[illegible]





US ARMY CORPS OF ENGINEERS JAPAN DISTRICT, OKINAWA AREA OFFICE USED-3 UNIT 35 532 APO, IA 96319-5322	DESIGNED BY: DRAWN BY: CHECKED BY: SUBMITTED BY: SIZE: ISO A1	SCALE: AS SHOWN	FILE NAME: HONOLULU, HAWAII 96817	ISO DATE:
---	--	--------------------	--------------------------------------	-----------

KADENA AIR BASE, OKINAWA, JAPAN
VEHICLE MAINTENANCE SHOP
F120 MCA PN77833



SHEET ID

E-721

— P
— O
— N
— M
— L
— K
— J
— I
— H
— G
— F
— E
— D
— C
— B
— A

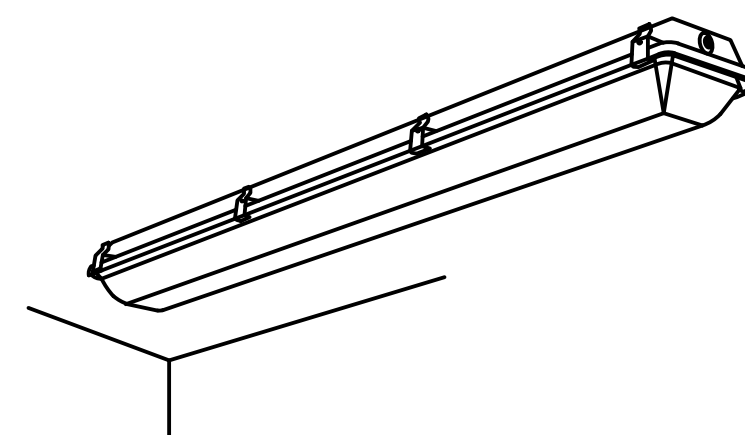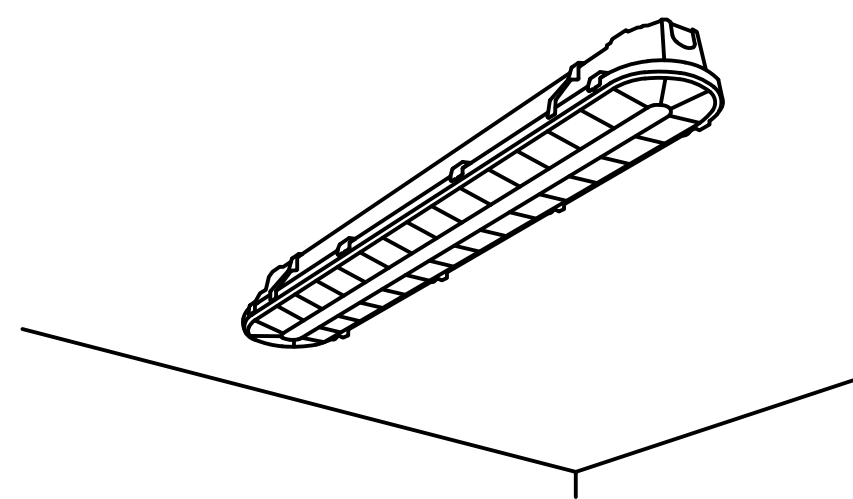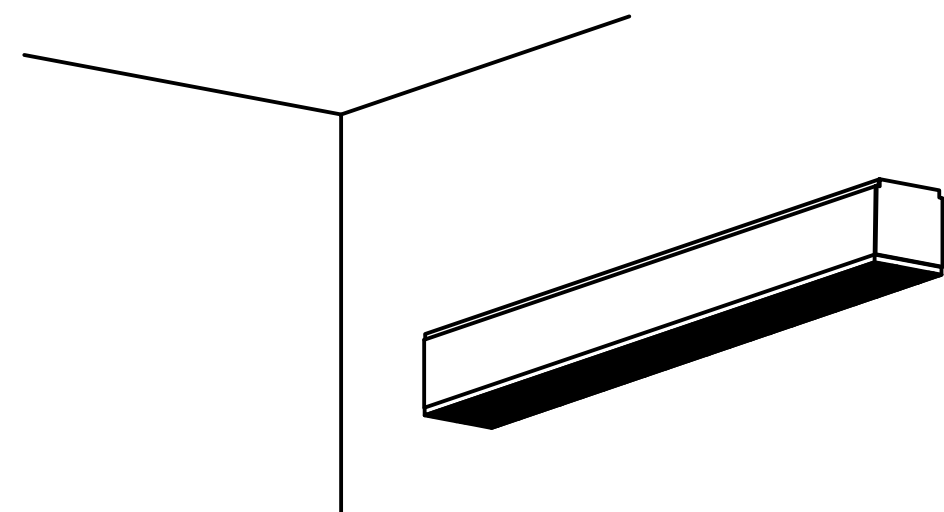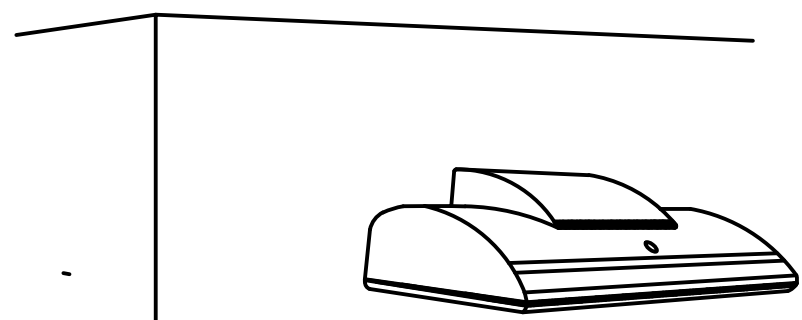

TYPE	LAMP & WATTS	MOUNTING	DESCRIPTION	
I	25W LED	WALL SURFACE	WALL PACK, 3000K, MINIMUM 70 CRI UON, HIGH-EFFICIENCY DIMMABLE DRIVER, UNIVERSAL VOLTAGE, UL LISTED FOR WET LOCATION, SURFACE MOUNTED WITH STAINLESS STEEL MOUNTING HARDWARE.	J	25W LED	WALL SURFACE	1200L WALL MOUNTED LINEAR, 3500K, MINIMUM 80 CRI UON, HIGH-EFFICIENCY DIMMABLE DRIVER, UNIVERSAL VOLTAGE, UL LISTED FOR DRY OR DAMP LOCATION, WALL SURFACE MOUNTED.	K	50W LED	WALL SURFACE	1200L, HIGH-IMPACT RESISTANT, FULLY GASKETED, 3500K, MINIMUM 80 CRI UON, HIGH-EFFICIENCY DIMMABLE DRIVER, UNIVERSAL VOLTAGE, UL LISTED FOR WET LOCATION, CEILING OR WALL SURFACE MOUNTED.	L	50W LED	CEILING, WALL SURFACE	1200L, HIGH-IMPACT RESISTANT, FULLY GASKETED, 3500K, MINIMUM 80 CRI UON, HIGH-EFFICIENCY DIMMABLE DRIVER, UNIVERSAL VOLTAGE, UL LISTED FOR WET LOCATION, UL LISTED FOR CLASS 1 DIVISION 2 HAZARDOUS LOCATIONS, CEILING OR WALL SURFACE MOUNTED.

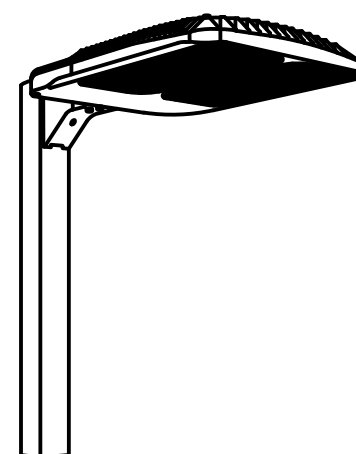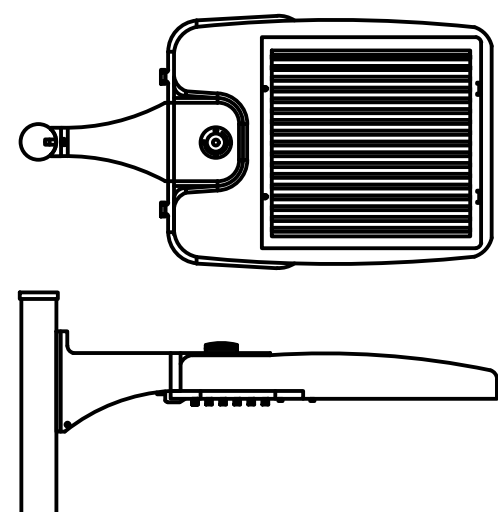

TYPE	LAMP & WATTS	MOUNTING	DESCRIPTION	TYPE	LAMP & WATTS	MOUNTING	DESCRIPTION	TYPE	LAMP & WATTS	MOUNTING	DESCRIPTION
M	161W LED	WALL SURFACE	LED AREA LUMINAIRE, UNIVERSAL VOLTAGE, UL LISTED FOR WET LOCATION, WALL SURFACE MOUNTED, INTEGRAL PHOTOCELL AND MOTION SENSOR.	N	215W LED	CEILING, SURFACE	LED PARKING LOT LUMINAIRE, UNIVERSAL VOLTAGE, UL LISTED FOR WET LOCATION, ARM-MOUNTED ON POLE, INTEGRAL PHOTOCELL AND MOTION SENSOR.	X	2W LED	CEILING, SURFACE	EXIT SIGN, UNIVERSAL VOLTAGE, UL LISTED FOR DAMP OR WET LOCATION, SURFACE MOUNTED ON CEILING AND/OR WALL, GREEN LETTERING WITH CHEVRONS, ONE- OR TWO-SIDED.

US Army Corps
of Engineers®[illegible]

US ARMY CORPS OF ENGINEERS JAPAN DISTRICT, OKINAWA AREA OFFICE WHEELER HALL, 352 APO, AP 96327-5132	DESIGNED BY: DRAWN BY: CHECKED BY: SUBMITTED BY: SIZE:	ISSUE DATE: SOLICITATION NO.: CONTRACT NO.: SCALE: FILE NAME:
--	--	---

KADENA AIR BASE, OKINAWA, JAPAN
VEHICLE MAINTENANCE SHOP
FYZO MCA PM77835

LUMINAIRE SCHEDULES

SHEET ID
E-722

INTERMEDIATE DESIGN

[illegible]

[illegible]

[illegible]

[illegible]

[illegible]

SITE TELECOMMUNICATIONS GENERAL ELECTRICAL NOTES:

1. INSTALLATION OF SITE TELECOMMUNICATIONS PATHWAYS AND INFRASTRUCTURE SHALL COMPLY WITH THE NATIONAL ELECTRICAL CODE (NEC), THE NATIONAL ELECTRICAL SAFETY CODE, THE APPLICABLE SECTIONS OF THE UNIFIED FACILITIES CRITERIA, AND THE APPLICABLE STANDARDS OF THE TELECOMMUNICATIONS INDUSTRY ASSOCIATION (TIA), UNLESS OTHERWISE NOTED.
 2. THE EXISTING CONDITIONS OF BELOW GROUND PIPING AND UTILITIES SUCH AS WATER MAINS, SANITARY SEWERS, STORM SEWERS, FUEL LINES, ELECTRICAL CONDUITS, COMMUNICATION CONDUITS AND OTHER UTILITIES ARE TAKEN FROM EXISTING RECORD DRAWINGS AND VERIFIED BY LIMITED FIELD OBSERVATION. IT SHALL BE THE CONTRACTORS' RESPONSIBILITY TO FIELD VERIFY THE EXACT LOCATION AND DEPTH OF BELOW GROUND PIPING AND UTILITIES IN THE IMMEDIATE VICINITY OF SUBSURFACE WORK, WHETHER SHOWN ON THE DRAWINGS OR NOT. CONTRACTOR SHALL MARK ALL EXISTING PIPING AND UTILITIES AFFECTED BY THE WORK USING UNDERGROUND MAP LOCATOR POSITION OF PIPES AND CONDUITS ON THE SURFACE. CONTRACTOR SHALL CONTACT THE UTILITIES REPRESENTATIVE 10 DAYS IN ADVANCE FOR ASSISTANCE IN MARKING OUT THE AREAS INVOLVING SUBSURFACE WORK. CONTRACTOR SHALL ADD THE EXISTING UNDERGROUND UTILITIES FOUND DURING PRELIMINARY STAKING TO DRAWINGS FOR RECORD. CONTRACTOR SHALL BE RESPONSIBLE FOR ANY AND ALL DAMAGES WHICH MIGHT OCCUR DUE TO THE CONTRACTOR'S FAILURE TO EXACTLY LOCATE AND PRESERVE ANY AND ALL UNDERGROUND UTILITIES. SUBMIT SHUTDOWN/OUTAGE SCHEDULE IN A TIMELY MANNER TO THE OWNER'S REPRESENTATIVE IN SUFFICIENT TIME TO SUBMIT AN OUTAGE REQUEST.
 3. CONDUIT BENDING CRITERIA:
 - A. THERE SHALL BE NO MORE THAN TWO 90-DEGREES BENDS OR A TOTAL OF 180 DEGREES BETWEEN MAINTENANCE HOLES, HANDHOLES, AND PULLBOXES.
 - B. FOR CONDUITS 2" IN DIAMETER OR SMALLER, MINIMUM RADIUS BENDS SHALL BE SIX TIMES THE DIAMETER OF THE CONDUIT.
 - C. FOR CONDUITS LARGER THAN 2" IN DIAMETER, MINIMUM RADIUS BENDS SHALL BE TEN TIMES THE DIAMETER OF THE CONDUIT.
 - D. ALL CONDUIT BENDS SHALL BE PRE-FORMED TYPE WHERE PRE-FORMED BENDS OF THE REQUIRED SIZES ARE AVAILABLE.
 - E. ALL CONDUIT BENDS REQUIRED DUE TO CHANGES IN GRADE SHALL HAVE A RADIUS BEND OF NOT LESS THAN 25 FEET (HORIZONTAL OR VERTICAL CHANGE).
 4. AFTER THE CONDUITS ARE INSTALLED BETWEEN UNDERGROUND STRUCTURES, A ROUND SOLID TEST MANDREL NOT LESS THAN 12" LONG AND HAVING A DIAMETER OF NO MORE THAN 1/4" LESS THAN THE DIAMETER OF THE CONDUIT SHALL BE PULLED THROUGH EACH CONDUIT AFTER WHICH A BRUSH WITH STIFF BRISTLES SHALL BE PULLED THROUGH TO MAKE CERTAIN THAT NO PARTICLES OF EARTH, SAND, OR GRAVEL HAVE BEEN LEFT IN THE CONDUIT. MANDREL TESTING MUST BE VERIFIED BY NAVFAC ET OR REPRESENTATIVE.
 5. AFTER THE CONDUITS ARE INSTALLED BETWEEN UNDERGROUND STRUCTURES AND BUILDING OR CABINET RISERS, A ROUND SOLID TEST MANDREL NOT LESS THAN 6" LONG AND HAVING A DIAMETER OF NO MORE THAN 1/4" LESS THAN THE DIAMETER OF THE CONDUIT SHALL BE PULLED THROUGH EACH CONDUIT AFTER WHICH A BRUSH WITH STIFF BRISTLES SHALL BE PULLED THROUGH TO MAKE CERTAIN THAT NO PARTICLES OF EARTH, SAND, OR GRAVEL HAVE BEEN LEFT IN THE CONDUIT. MANDREL TESTING MUST BE VERIFIED BY NAVFAC ET OR REPRESENTATIVE.
 6. MANDREL TEST RESULTS SHALL BE DOCUMENTED AND PROVIDED TO THE CONTRACTING OFFICER WITHIN 14 DAYS OF COMPLETING THE TESTS FOR DISSEMINATION TO THE BASE COMMUNICATIONS OFFICE. MANDREL TESTING MUST BE VERIFIED BY NAVFAC ET OR REPRESENTATIVE.
 7. PROVIDE 3 SETS OF 3-CELL, 3" PER CELL, FLEXIBLE FABRIC INNER DUCTS IN A MINIMUM OF 50% OF NEW 4" DUCTS. INSTALL POLYESTER PULL ROPE IN ALL NEW CONDUITS AND CAP ALL CONDUITS AFTER TESTING. THE POLYESTER PULL ROPE SHALL BE PRE-LUBRICATED AND PRINTED WITH SEQUENTIAL FOOTAGE MARKINGS. FOR DUCT SYSTEMS WITH MULTIPLE ROWS, THE TOP ROWS SHALL BE PROVIDED WITH INNERDUCTS. EX: FOR A 2X2 DUCT INSTALLATION, FILL THE TOP TWO DUCTS WITH INNERDUCT.
 8. ALL CONDUITS SHALL ENTER UNDERGROUND STRUCTURES AT 90 DEGREE ANGLES AND SHALL BE FLUSH WITH FLARED OR BELL ENDS TO PREVENT CABLE DAMAGE.
 9. ALL DUCTS ASSOCIATED WITH PULL BOXES OR MAINTENANCE HOLES SHALL BE INSTALLED WITH ADEQUATE DRAINAGE TOWARD THE PULLBOXES OR MAINTENANCE HOLES (MINIMUM ONE-FOURTH PERCENT SLOPE UNLESS OTHERWISE NOTED).
 10. ALL DUCTS AND MAINTENANCE HOLES SHALL BE INSPECTED AND ACCEPTED BY THE GOVERNMENT A MINIMUM OF 30 DAYS PRIOR TO SERVICE REQUIRED DATE.
 11. ALL DUCTLINES SHALL BE CONCRETE ENCASED, UNLESS SPECIFICALLY IDENTIFIED OTHERWISE.
 12. UNDERGROUND CONDUIT SHALL BE PVC SCHEDULE 40, INSTALLED A MINIMUM OF 24" BELOW FINISHED GRADE, UNLESS OTHERWISE NOTED ABOVE GROUND CONDUIT SHALL BE GALVANIZED RIGID STEEL (UP TO 10' AFF) OR EMT (ABOVE 10' AFF).
 13. ALL SPARE CONDUITS SHALL BE SEALED TO PREVENT ENTRANCE OF MOISTURE, GASES, AND RODENTS.
 14. ALL OSP UNDERGROUND FIBER OPTIC CABLE SHALL BE ARMORED.
 15. PROVIDE A MINIMUM 50 FOOT MAINTENANCE LOOP FOR ALL CABLES IN THE LAST MAINTENANCE HOLE FEEDING INTO BUILDING ENTRANCE FACILITIES.
 16. PROVIDE CABLE TAGS FOR EACH TELECOMMUNICATIONS CABLE OR WIRE LOCATED IN MAINTENANCE HOLES, HANDHOLES, AND VAULTS IN ACCORDANCE WITH APPLICABLE TIA STANDARD.
 17. EXTERIOR MOUNTED EQUIPMENT SHALL BE PROVIDED WITH A WEATHERPROOF, NEMA 4X TYPE 316 STAINLESS STEEL ENCLOSURE.
 18. COORDINATE TELECOMMUNICATIONS WORK WITH ALL OTHER TRADES.
 19. ALL TELECOMMUNICATIONS WORK MUST BE IN ACCORDANCE WITH APPLICABLE STANDARDS OF THE TELECOMMUNICATIONS INDUSTRY ASSOCIATION (TIA), BUILDING INDUSTRY CONSULTING SERVICES INTERNATIONAL (BICSI), APPLICABLE SECTIONS OF NATIONAL ELECTRICAL CODE (NEC), AND THE NATIONAL ELECTRICAL SAFETY CODE (NESC).

BUILDING TELECOMMUNICATIONS GENERAL NOTES:

1. INSTALLATION OF INTERIOR TELECOMMUNICATIONS PATHWAYS AND INFRASTRUCTURE SHALL COMPLY WITH THE NATIONAL ELECTRICAL CODE (NEC), THE NATIONAL ELECTRICAL SAFETY CODE, THE APPLICABLE SECTIONS OF THE UNIFIED FACILITIES CRITERIA, AND THE APPLICABLE STANDARDS OF THE TELECOMMUNICATIONS INDUSTRY ASSOCIATION (TIA), UNLESS OTHERWISE NOTED.
2. FURNISH AND INSTALL ALL JUNCTION AND PULLBOXES REQUIRED FOR THE INSTALLATION OF DEVICES AND EQUIPMENT, WHETHER OR NOT SPECIFICALLY INDICATED ON THE PLANS. SIZE PULLBOXES PER THE APPLICABLE TIA STANDARDS, IF NOT OTHERWISE INDICATED ON THE DRAWINGS. ALL JUNCTION AND PULLBOXES SHALL BE READILY ACCESSIBLE.
3. NO SECTION OF CONDUIT SHALL BE LONGER THAN 100 FEET WITHOUT A PULLBOX. A PULLBOX SHALL BE PLACED IN A CONDUIT RUN WHERE THE LENGTH IS OVER 100 FEET, THERE ARE MORE THAN TWO 90 DEGREE BENDS, OR EQUIVALENT, OR THERE IS A REVERSE (U-SHAPED) BEND IN THE RUN. PULLBOXES SHALL BE PLACED IN A STRAIGHT SECTION OF CONDUIT AND SHALL NOT BE USED IN LIEU OF A BEND.
4. CONDUIT RUNS SHOWN ARE DIAGRAMMATIC ONLY. INSTALL ALL CONDUITS TO SUIT FIELD CONDITIONS.
5. MINIMUM CONDUIT SIZE SHALL BE 1" C, UNLESS OTHERWISE NOTED.
6. CONDUIT BENDING CRITERIA:
 - A. FOR CONDUITS 2" IN DIAMETER OR SMALLER, MINIMUM RADIUS BENDS SHALL BE SIX TIMES THE DIAMETER OF THE CONDUIT.
 - B. FOR CONDUITS LARGER THAN 2" IN DIAMETER, MINIMUM RADIUS BENDS SHALL BE TEN TIMES THE DIAMETER OF THE CONDUIT.
 - C. ALL CONDUIT BENDS SHALL BE PRE-FORMED TYPE WHERE PRE-FORMED BENDS OF THE REQUIRED SIZES ARE AVAILABLE.
7. PROVIDE INSULATED BUSHINGS AT ALL TELECOMMUNICATIONS CONDUIT TERMINATIONS AT ALL BOXES AND CONDUIT STUBS.
8. CONDUIT FILL SHALL BE IN ACCORDANCE WITH THE APPLICABLE TIA STANDARDS.
9. THE MAXIMUM FILL RATIO OF ANY CABLE TRAY SHALL BE 50%. THE MAXIMUM FILL DEPTH OF ANY CABLE TRAY SHALL BE 6 INCHES IN ACCORDANCE WITH THE APPLICABLE TIA STANDARDS.
10. ALL TELECOMMUNICATION CONDUITS OUTSIDE THE TELECOMMUNICATION ROOMS OR CLOSETS SHALL BE CONCEALED EITHER ABOVE SUSPENDED CEILINGS, EMBEDDED IN CONCRETE OR BELOW CONCRETE FLOORS OR CEILING STRUCTURES. JUNCTION BOXES FOR CONDUITS ABOVE DRYWALL CEILINGS SHALL BE ACCESSIBLE BY CEILING ACCESS POINTS.
11. ALL CABLE PATHWAYS INCLUDING CONDUITS, PULLBOXES, AND JUNCTION BOXES SHALL BE PROVIDED WITH LABELS THAT STATE WHERE THEY ORIGINATE AND TERMINATE. PULLBOXES AND JUNCTION BOXES SHALL BE NUMBERED IN SEQUENCE FROM THE TELECOM ROOM OUTWARDS. ALL CONDUITS, EMPTY OR USED, SHALL BE CLEARLY AND PERMANENTLY MARKED AT BOTH ENDS, TO INDICATE DESTINATION. MARKING MUST BE CLEARLY VISIBLE AFTER CONSTRUCTION IS COMPLETED.
12. ALL CONDUITS ENTERING THE BUILDING FROM THE EXTERIOR SHALL BE SEALED TO PREVENT ENTRANCE OF MOISTURE, GASES, AND RODENTS.
13. SEAL ALL PENETRATIONS THROUGH FIRE RATED WALLS AND SLABS USING A U.L. LISTED FIRE RATED SEALANT OR ASSEMBLY TO MAINTAIN THE INTEGRITY OF THE FIRE RATING.
14. OUTLET BOXES IN FIRE RATED WALLS SHALL HAVE A MINIMUM SEPARATION OF 24" FROM ANY OUTLET BOXES ON THE OPPOSITE SIDE OF SAME WALL, UNLESS ALLOWED OTHERWISE BY BUILDING CODES.
15. PROVIDE GROUNDING AND BONDING FOR THE TELECOMMUNICATIONS SYSTEM INSTALLATION PER THE NEC AND THE APPLICABLE TIA STANDARDS.
16. ALL NON-CURRENT CARRYING METAL PARTS OF EQUIPMENT RACKS AND SUPPORTING STRUCTURES (CABLE TRAYS, CONDUITS, ETC.) SHALL BE BONDED TO THE TELECOM ROOM SIGNAL GROUND PER THE APPLICABLE TIA STANDARDS.
17. EXTERIOR MOUNTED EQUIPMENT SHALL BE PROVIDED WITH A WEATHERPROOF, NEMA 4X TYPE 316 STAINLESS STEEL ENCLOSURE.
18. INSTALL ALL EQUIPMENT, DEVICES, CONDUIT AND CONDUIT SUPPORTS TO MEET THE PROJECT LOCATION'S SEISMIC RESTRAINT REQUIREMENTS.
19. UNLESS SHOWN OTHERWISE, PROVIDE TREATED, FIRE RATED PLYWOOD BACKBOARDS ON A MINIMUM OF 2 WALLS IN EACH TELECOM ROOM.
20. CATEGORY 6/6A CABLEING SHALL BE INSTALLED WITH SLACK AT BOTH TERMINATING ENDS AND SHALL BE CONFIGURED TO T568C STANDARDS.



U.S. Army Corps
Engineers®





[illegible]

JAPAN DISTRICT OKINAWA AREA OFFICE		SOLICITATION NO.:	
USAED-J Unit 35132		DRAWN BY:	
APO, AP 96374-5132		CHECKED BY:	
 SSPM INTERNATIONAL, INC. 501 KALANAN KUAH RD #20 HONOLULU, HAWAII 96817		CONTRACT NO.:	
		SUBMITTED BY:	
		SCALE: AS SHOWN	
SIZE:		FILE NAME:	
ISO A1			

MADEIRA BASE, OKINAWA, JAPAN
VEHICLE MAINTENANCE SHOP
FY20 MCA PN77833

HEET ID

Г-001

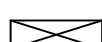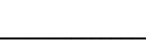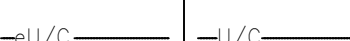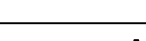COMMUNICATION LEGEND		
EXIST	NEW	DESCRIPTION
		JUNCTION BOX, WALL MOUNTED
		JUNCTION BOX, CEILING MOUNTED
		CABLE TELEVISION OUTLET, BLONDER TONGUE VERSASTAP V-1GT-FT W/ F-CONNECTOR IN 4-11/16Sqx2.5"D JB, MOUNTED @+96" AFF, OFFSET 12-16" FROM CTR OF WHITEBOARD OR AS INDICATED
		COMMUNICATION OUTLET, 4-POSITION W/ (3) RJ45 JACKS (TIA/EIA-568B), 4-11/16"Sq x2.5"D JB W/ 2-GANG COVER PLATE, 1"C STUBBED OUT TO CABLE TRAY W/ (3) CAT 6 CABLES. MOUNTED @+18" AFF.
		COMMUNICATION OUTLET, 4-POSITION W/ (3) RJ45 JACKS (TIA/EIA-568B), 4-11/16"Sq x2.5"D JB W/ 2-GANG COVER PLATE, 1"C STUBBED OUT TO CABLE TRAY W/ (3) CAT 6 CABLES. MOUNTED @+96" AFF.
		COMMUNICATION OUTLET, 4-POSITION W/ (3) RJ45 JACKS (TIA/EIA-568B), 4-11/16"Sq x2.5"D JB W/ 2-GANG COVER PLATE, 1"C STUBBED OUT TO CABLE TRAY W/ (3) CAT 6 CABLES. MTD @+6" ABOVE COUNTER.
		WAP OUTLET, 4-POSITION W/ (3) RJ45 JACKS (TIA/EIA-568B), 4-11/16"Sq x2.5"D JB W/ 2-GANG COVER PLATE, 1"C STUBBED OUT TO CABLE TRAY W/ (3) CAT 6 CABLES. MOUNTED @+96" AFF.
		WAP OUTLET, 4-POSITION W/ (2) RJ45 JACKS (TIA/EIA-568B), 4-11/16"Sq x2.5"D JB W/ 2-GANG COVER PLATE, 1"C STUBBED OUT TO CABLE TRAY W/ (3) CAT 6 CABLES. CEILING MOUNTED.
		TELEPHONE OUTLET, RJ-11 JACK, 3/4"C STUBBED OUT TO CABLE TRAY W/ (1) CAT 6 CABLES, MOUNTED @+48" AFF OR AS INDICATED
		COMMUNICATION OUTLET, 4-POSITION W/ (3) RJ45 JACKS (TIA/EIA-568B), 1"C STUBBED OUT TO CABLE TRAY W/ (3) CAT 6 CABLES. FLOOR MOUNTED.
		IP SPEAKER OUTLET, 2-POSITION W/ (2) RJ45 JACKS (TIA/EIA-568B), 4-11/16"Sq x2.5"D JB W/ 2-GANG COVER PLATE, 1"C STUBBED OUT TO CABLE TRAY W/ (2) CAT 6 CABLES. MOUNTED @+96" AFF OR AS NOTED.
		IP SPEAKER OUTLET, 2-POSITION W/ (2) RJ45 JACKS (TIA/EIA-568B), 4-11/16"Sq x2.5"D JB W/ 2-GANG COVER PLATE, 1"C STUBBED OUT TO CABLE TRAY W/ (2) CAT 6 CABLES. CEILING MOUNTED.
		IP EXTERIOR SPEAKER OUTLET, 2-POSITION W/ (2) RJ45 JACKS (TIA/EIA-568B), 4-11/16"Sq x2.5"D JB W/ 2-GANG COVER PLATE, 1"C STUBBED OUT TO CABLE TRAY W/ (2) CAT 6 CABLES. MOUNTED @+96" AFF OR AS NOTED.
		WALL MOUNTED COMM RACK
		CABLE TRAY
		CONCEALED COMMUNICATION CONDUIT UNLESS OTHERWISE NOTED.
		EXPOSED COMMUNICATION CONDUIT UNLESS OTHERWISE NOTED.
		CONDUIT STUB OUT WITH PLASTIC BUSHING
		UNDER CONCRETE SLAB COMMUNICATION CONDUIT
		UNDERGROUND COMMUNICATION DUCT
		SPEAKER CABLE IN CONDUIT
		DUCT SECTION INDICATOR.
		INDICATES WORK NOTE

TELECOMMUNICATION ABBREVIATION	
18"	DENOTES 18" ABOVE FINISHED FLOOR OR GRADE
AACS	AUTOMATED ACCESS CONTROL SYSTEM
AMI	ADVANCED METERING INFRASTRUCTURE
A.F.F.	ABOVE FINISHED FLOOR
A/V	AUDIO VISUAL
CAT6	CATEGORY 6
CTR	COMMERCIAL TELECOMMUNICATIONS ROOM
DDC	DIRECT DIGITAL CONTROL
EMT	ELECTRICAL METAL TUBING
ESS	ELECTRONIC SECURITY SYSTEM
F/UTP	FOILED UNSHIELDED TWISTED PAIR
FRCS	FACILITY RELATED CONTROL SYSTEMS
GE	GROUNDING EQUALIZER
GFGI	GOVERNMENT FURNISHED GOVERNMENT INSTALLED
GND	GROUND
GTR	GOVERNMENT TELECOMMUNICATIONS ROOM
ICS	INDUSTRIAL CONTROL SYSTEMS
IDS	INTRUSION DETECTION SYSTEM
JB	JUNCTION BOX
MAX	MAXIMUM
MIN	MINIMUM
MM	MULTIMODE
NIC	NOT IN CONTRACT
NIPR	NON-SECURE INTERNET PROTOCOL
OSP	OUTSIDE PLANT
PBB	PRIMARY BONDING BUSBAR
PET	PROTECTED ENTRANCE TERMINAL (SAME AS BET)
POTS	PLAIN OLD TELEPHONE SERVICE
RBB	RACK BONDING BUSBAR
RBC	RACK BONDING CONDUCTOR
RCDD	REGISTERED COMMUNICATIONS DISTRIBUTION DESIGNER
SBB	SECONDARY BONDING BUSBAR
SM	SINGLE MODE
TBB	TELECOMMUNICATIONS BONDING BACKBONE
TBC	TELECOMMUNICATIONS BONDING CONDUCTOR
TEBC	TELECOMMUNICATIONS EQUIPMENT BONDING CONDUCTOR
THH	TELECOMMUNICATION HANDHOLE
TMH	TELECOMMUNICATION MAINTENANCE HOLE
TR	TELECOMMUNICATION ROOM
TYP	TYPICAL
UTP	UNSHIELDED TWISTED PAIR
WAP	WIRELESS ACCESS POINT
WP	WEATHER PROOF

SHEET ID

T-002

TELECOMMUNICATIONS SYMBOL LIST AND ABBREVIATION

KADENA AIR BASE, OKINAWA, JAPAN
VEHICLE MAINTENANCE SHOP
FY20 MCA PN7833

DESIGNED BY:

US ARMY CORPS OF ENGINEERS

JAPAN DISTRICT, OKINAWA AREA OFFICE

USAED-J, UNIT 35132

CHECKED BY:

APO, AP 96374-5132

DRAWN BY:

ISSUED DATE:

SOLICITATION NO.:

CONTRACT NO.:

SUBMITTED BY:

SCALE:

AS SHOWN

SIZE:

ISO A1

FILE NAME:

MARK:


DESCRIPTION

DATE

P
O
N
M
L
K
J
I
H
G
F
E
D
C
B
A

SEE SHEET TD102
FOR DETAILS

SEE SHEET TD103
FOR DETAILS

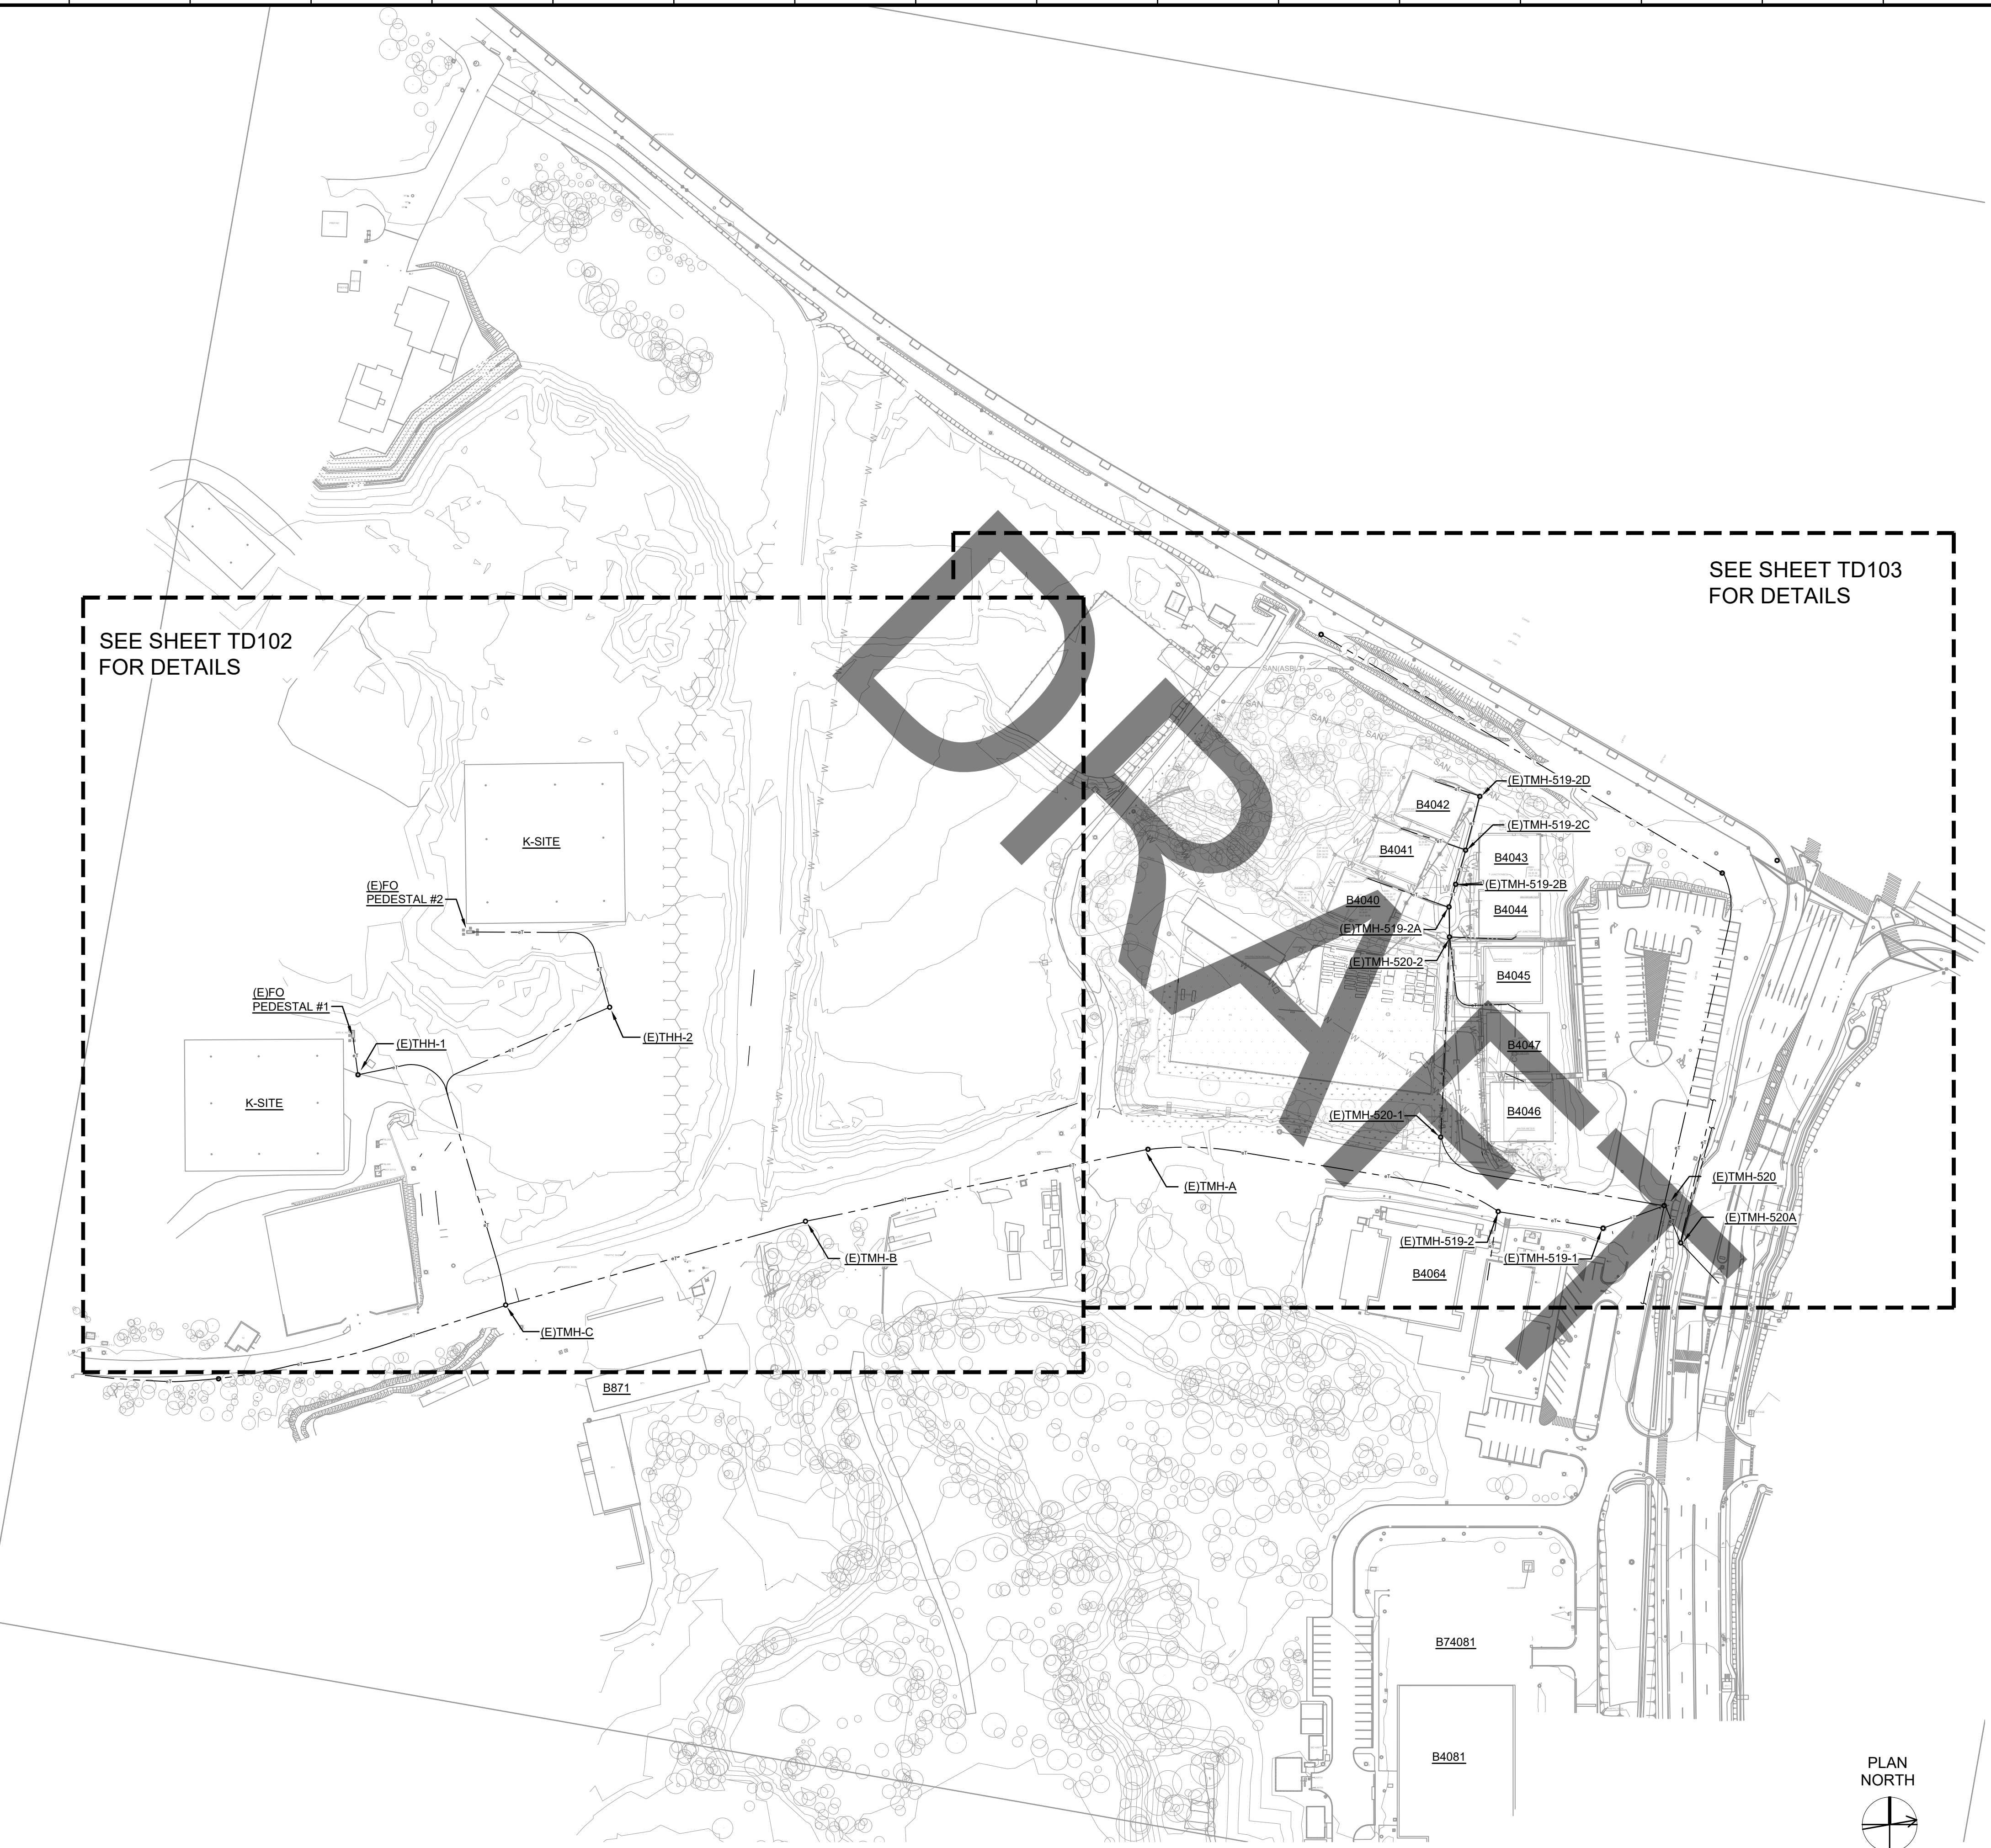

A1 OVERALL SITE TELECOMMUNICATION DEMOLITION PLAN (CLIN0001 - CLIN0003)
1:1000

GENERAL NOTES

1. SEE CIVIL AND ELECTRICAL PLANS FOR SITE DEMOLITION WORK AND CLOSELY COORDINATE THE DEMOLITION WORK FOR TELECOMMUNICATIONS SYSTEMS.
2. PRIOR TO ANY TELECOMMUNICATIONS INFRASTRUCTURE AND CABLE DEMOLITION WORK, ENSURE THAT THE NEW INFRASTRUCTURE AND CABLES ARE ESTABLISHED TO MINIMIZE DISRUPTION TO THE OPERATIONS OF THE EXISTING FACILITIES.
3. THE CONTRACTOR SHALL BE RESPONSIBLE TO SUBMIT A PROPOSED PHASING SCHEME IN COORDINATION WITH CIVIL AND ELECTRICAL WORK FOR REVIEW AND APPROVAL PRIOR TO START OF DEMOLITION WORK.

KEY NOTES

CLIN 0001-0003

- CLIN 0001:**
- SITE PREPARATION WORK FOR VMS FACILITIES.
 - LOONEY STREET AND ELECTRICAL AND TELECOMMUNICATIONS INFRASTRUCTURE IMPROVEMENTS.
 - CONSTRUCTION OF CABLE HUT, RELOCATION OF COMMUNICATIONS HUB FOR CRITICAL OPTICAL FIBER AND COPPER CABLES FROM B4040, AND REESTABLISH THE SERVICES.
 - ENSURE THAT TELECOMMUNICATION SERVICES TO EXISTING ADA BUILDINGS (B4040 THRU B4047) ARE MAINTAINED.
 - RESTORE OPTICAL FIBER CABLES TO K-SITES FROM NEW CABLE HUT.
 - CONSTRUCTION OF VEHICLE MAINTENANCE SHOP, FIRE PUMP HOUSE, WATER STORAGE TANK, AND ASSOCIATED TELECOMMUNICATIONS INFRASTRUCTURE.
- CLIN 0002:**
- CONSTRUCTION OF ORGANIZATIONAL EQUIPMENT STORAGE, POL STORAGE, AND ASSOCIATED TELECOMMUNICATIONS INFRASTRUCTURE.
- CLIN 0003:**
- CONSTRUCTION OF ORGANIZATIONAL VEHICLE PARKING LOT.
 - CONSTRUCTION OF WASH RACK.

US Army Corps
of Engineers®

ISSUE DATE:		SOLICITATION NO.:		CONTRACT NO.:		SCALE:		AS SHOWN		FILE NAME:	
DESIGNED BY:		DRAWN BY:		CHECKED BY:		SUBMITTED BY:		SIZE:	ISO A1	MARK	DESCRIPTION
US ARMY CORPS OF ENGINEERS JAPAN DISTRICT, OKINAWA AREA OFFICE USAED-J UNIT 35132 APO, AP 96374-5132		SSFM INTERNATIONAL, INC. 501 SUMNER STREET, SUITE 620 HONOLULU, HAWAII 96817									

KADENA AIR BASE, OKINAWA, JAPAN
VEHICLE MAINTENANCE SHOP
FY20 MCA PN77833

OVERALL SITE TELECOM DEMOLITION PLAN (CLIN 0001 - CLIN 0003)

SHEET ID

TS101

INTERMEDIATE DESIGN

P
O
N
M
L
K
J
I
H
G
F
E
D
C
B
A

DUCT CABLE SCHEDULE				
TAG	DUCTS	CABLES		REMARKS
(a)	(2) 104mm EXIST	P50-24FF CA07:301-325+ A,26-50	12SM FOC FR B4040 F.O. LINK B4042	EXIST CABLES TO REMAIN
(b)	(2) 104mm EXIST	P50-24FF CA07:276-300+ A,26-50	12SM FOC FR B4040 F.O. LINK B4041	EXIST CABLES TO REMAIN
(c)	(2) 104mm EXIST	P50-24FF CA07:326-350+ A,26-50	12SM FOC FR B4040 F.O. LINK B4043	EXIST CABLES TO REMAIN
(d)	(2) 104mm EXIST	P50-24FF CA07:351-375+ A,26-50	12SM FOC FR B4040 F.O. LINK B4044	EXIST CABLES TO REMAIN
(e)	(2) 104mm EXIST	P50-24FF CA07:176-200+ A,26-50 P50-24FF CA07:201-225+ A,26-50 P50-24FF CA07:226-250+ A,26-50	12SM FOC FR B4040 F.O. LINK B4045 12SM FOC FR B4040 F.O. LINK B4047 12SM FOC FR B4040 F.O. LINK B4046	EXIST CABLES TO REMAIN
(f)	(2) 104mm EXIST	P50-24FF CA07:201-225+ A,26-50 P50-24FF CA07:226-250+ A,26-50	12SM FOC FR B4040 F.O. LINK B4047 12SM FOC FR B4040 F.O. LINK B4046	EXIST CABLES TO REMAIN
(g)	(2) 104mm EXIST	P50-24FF CA07:226-250+ A,26-50	12SM FOC FR B4040 F.O. LINK B4046	EXIST CABLES TO REMAIN
(h)	(4) 104mm EXIST	P6-24FF CA07:176-600+ A,1-175	144SM FOC B4040-TMH510 144SM FOC FRROM B718 F.O. LINK B4040, 13-144 (+1-12DD)	EXIST FO CABLES TO BE REPLACED
(i)	(4) 104mm EXIST (2) 104mm EXIST	P6-24FF CA09:1-62+ 151-300+ 401-600+ A, 301-400+ B, 86-100+ C, 101-150+ D, 63-87 P25-24FF CAJ20:976-1000	48S08F F.O. LINK 10-9-1-48 B926 TO B4065 1-12 STRD SM FOC (FO PEDESTAL #1) 1-12 STRD SM FOC (FO PEDESTAL #2)	EXIST CABLES TO REMAIN
(j)	(3) 104mm EXIST	P50-24FF CA09:501-550	48S08F F.O. LINK 10-9-1-48 B926 TO B4065	EXIST CABLES TO REMAIN
(k)	(2) 104mm EXIST		1-12 STRD SM FOC (FO PEDESTAL #1) 1-12 STRD SM FOC (FO PEDESTAL #2)	EXIST CABLES TO BE REPLACED
(l)	(6) 104mm TO (E)TMH-624	P12-22PEC CAJ20:1-975+ 1001-1200+ A,976-1000 12S08F F.O.LINK10-7B:1-12 BLDG973TOBLDG52200 12S08F F.O.LINK10-5A:1-6+ A,7-12 BLDG4081TOBLDG53115 CATV	24S10FN2 F.O.LINK4:1-12+ A,13-24 P2-24PF CA45:1-200 U.S.NAVY (N)12SM B3670-B6105	
(m)	(2) 104mm TO (E)TMH-223- 26-A	46L8.3F FO 926-6105,1-36+ FO 926-52200,34-48 144SM FOC B4040-TMH510		
(n)	(6) 104mm (4) 104mm	48S08F F.O.LINK10-9-1-48 BLDG926TOBLDG4065 12S08F F.O.LINK10-7B:1-12 BLDG973TOBLDG52200 P12-22PLAP CAJ20:1-1200 24S10F F.O.LINK4:1-12+ A,13-24 TMH510TOBLDG6105 12S08F F.O.LINK10-5A:1-6+ A,7-12 BLDG4081TOGATE3	P2-22PLAP CA45:1-200 P6-24FF FA09:1-87+ 151-300+ 401-600+ A,301-400+ B,86-100+ C,101-150 U.S.NAVY (N)12SM B3670-B6105 F.O.LINK BLDG4044: 13-144+1-12DD P6-24FF CA07:176-600+ P6-24FF CA07:176-600+ A,1-175	



GENERAL NOTES

- SEE CIVIL AND ELECTRICAL PLANS FOR SITE DEMOLITION WORK AND CLOSELY COORDINATE THE DEMOLITION WORK FOR TELECOMMUNICATIONS SYSTEMS.
- PRIOR TO ANY TELECOMMUNICATIONS INFRASTRUCTURE AND CABLE DEMOLITION WORK, ENSURE THAT THE NEW INFRASTRUCTURE AND CABLES ARE ESTABLISHED TO MINIMIZE DISRUPTION TO THE OPERATIONS OF THE EXISTING FACILITIES.
- THE CONTRACTOR SHALL BE RESPONSIBLE TO SUBMIT A PROPOSED PHASING SCHEME IN COORDINATION WITH CIVIL AND ELECTRICAL WORK FOR REVIEW AND APPROVAL PRIOR TO START OF DEMOLITION WORK.

KEY NOTES

- EXIST FO CABLE HUB LOCATED IN ADA B4040 SHALL BE RELOCATED TO A PROPOSED CABLE HUT AND ALL EXIST CRITICAL SERVICES SHALL BE RE-ESTABLISHED PRIOR TO DEMOLITION OF COMMUNICATION CABLES AND INFRASTRUCTURE.
- EXIST OPTICAL FIBER CABLES SERVING THE K-SITES SHALL BE REMOVED AND RESTORED BACK TO THE NEW CABLE HUT UTILIZING EXIST AND NEW INFRASTRUCTURE.
- EXISTING MAINTENANCE HOLES AND DUCTS SHALL BE SALVAGED AND REUSED. MODIFY MAINTENANCE HOLE FINISH TO MATCH THE FINAL GRADING.
- EXISTING TELECOMMUNICATION SERVICES TO ADA BUILDINGS (B4040 THRU B4047) SHALL REMAIN IN SERVICE BY RECONNECTING THE SERVER IN B4040 TO NEW CABLE HUT.

CLIN 0001-0003

- CLIN 0001:**
- SITE PREPARATION WORK FOR VMS FACILITIES.
 - LOONEY STREET AND ELECTRICAL AND TELECOMMUNICATIONS INFRASTRUCTURE IMPROVEMENTS.
 - CONSTRUCTION OF CABLE HUT, RELOCATION OF COMMUNICATIONS HUB FOR CRITICAL OPTICAL FIBER AND COPPER CABLES FROM B4040, AND REESTABLISH THE SERVICES.
 - ENSURE THAT TELECOMMUNICATION SERVICES TO EXISTING ADA BUILDINGS (B4040 THRU B4047) ARE MAINTAINED.
 - RESTORE OPTICAL FIBER CABLES TO K-SITES FROM NEW CABLE HUT.
 - CONSTRUCTION OF VEHICLE MAINTENANCE SHOP, FIRE PUMP HOUSE, WATER STORAGE TANK, AND ASSOCIATED TELECOMMUNICATIONS INFRASTRUCTURE.
- CLIN 0002:**
- CONSTRUCTION OF ORGANIZATIONAL EQUIPMENT STORAGE, POL STORAGE, AND ASSOCIATED TELECOMMUNICATIONS INFRASTRUCTURE.
- CLIN 0003:**
- CONSTRUCTION OF ORGANIZATIONAL VEHICLE PARKING LOT.
 - CONSTRUCTION OF WASH RACK.

US Army Corps of Engineers®

ISSUE DATE:	SOLICITATION NO.:	CONTRACT NO.:	DATE:
DESIGNED BY:	DRAWN BY:	CHECKED BY:	MARK:
ISSUED BY:	ISSUED BY:	ISSUED BY:	DESCRIPTION:
FILE NAME:	SCALE:	AS SHOWN	
SIZE:	ISO A1		

US ARMY CORPS OF ENGINEERS
JAPAN DISTRICT, OKINAWA AREA OFFICE
USAED-J UNIT 35132
APO, AP 96374-5132

SSEM
SSEM INTERNATIONAL, INC.
501 SUMNER STREET, SUITE 620
HONOLULU, HAWAII 96817

KADENA AIR BASE, OKINAWA, JAPAN
VEHICLE MAINTENANCE SHOP
FY20 MCA PN77833


PARTIAL SITE TELECOM DEMOLITION PLAN - (CLIN 0001 - CLIN 0003)

SHEET ID

TS103

INTERMEDIATE DESIGN

— P
— O
— N
— M
— L
— K
— J
— I
— H
— G
— F
— E
— D
— C
— B
— A

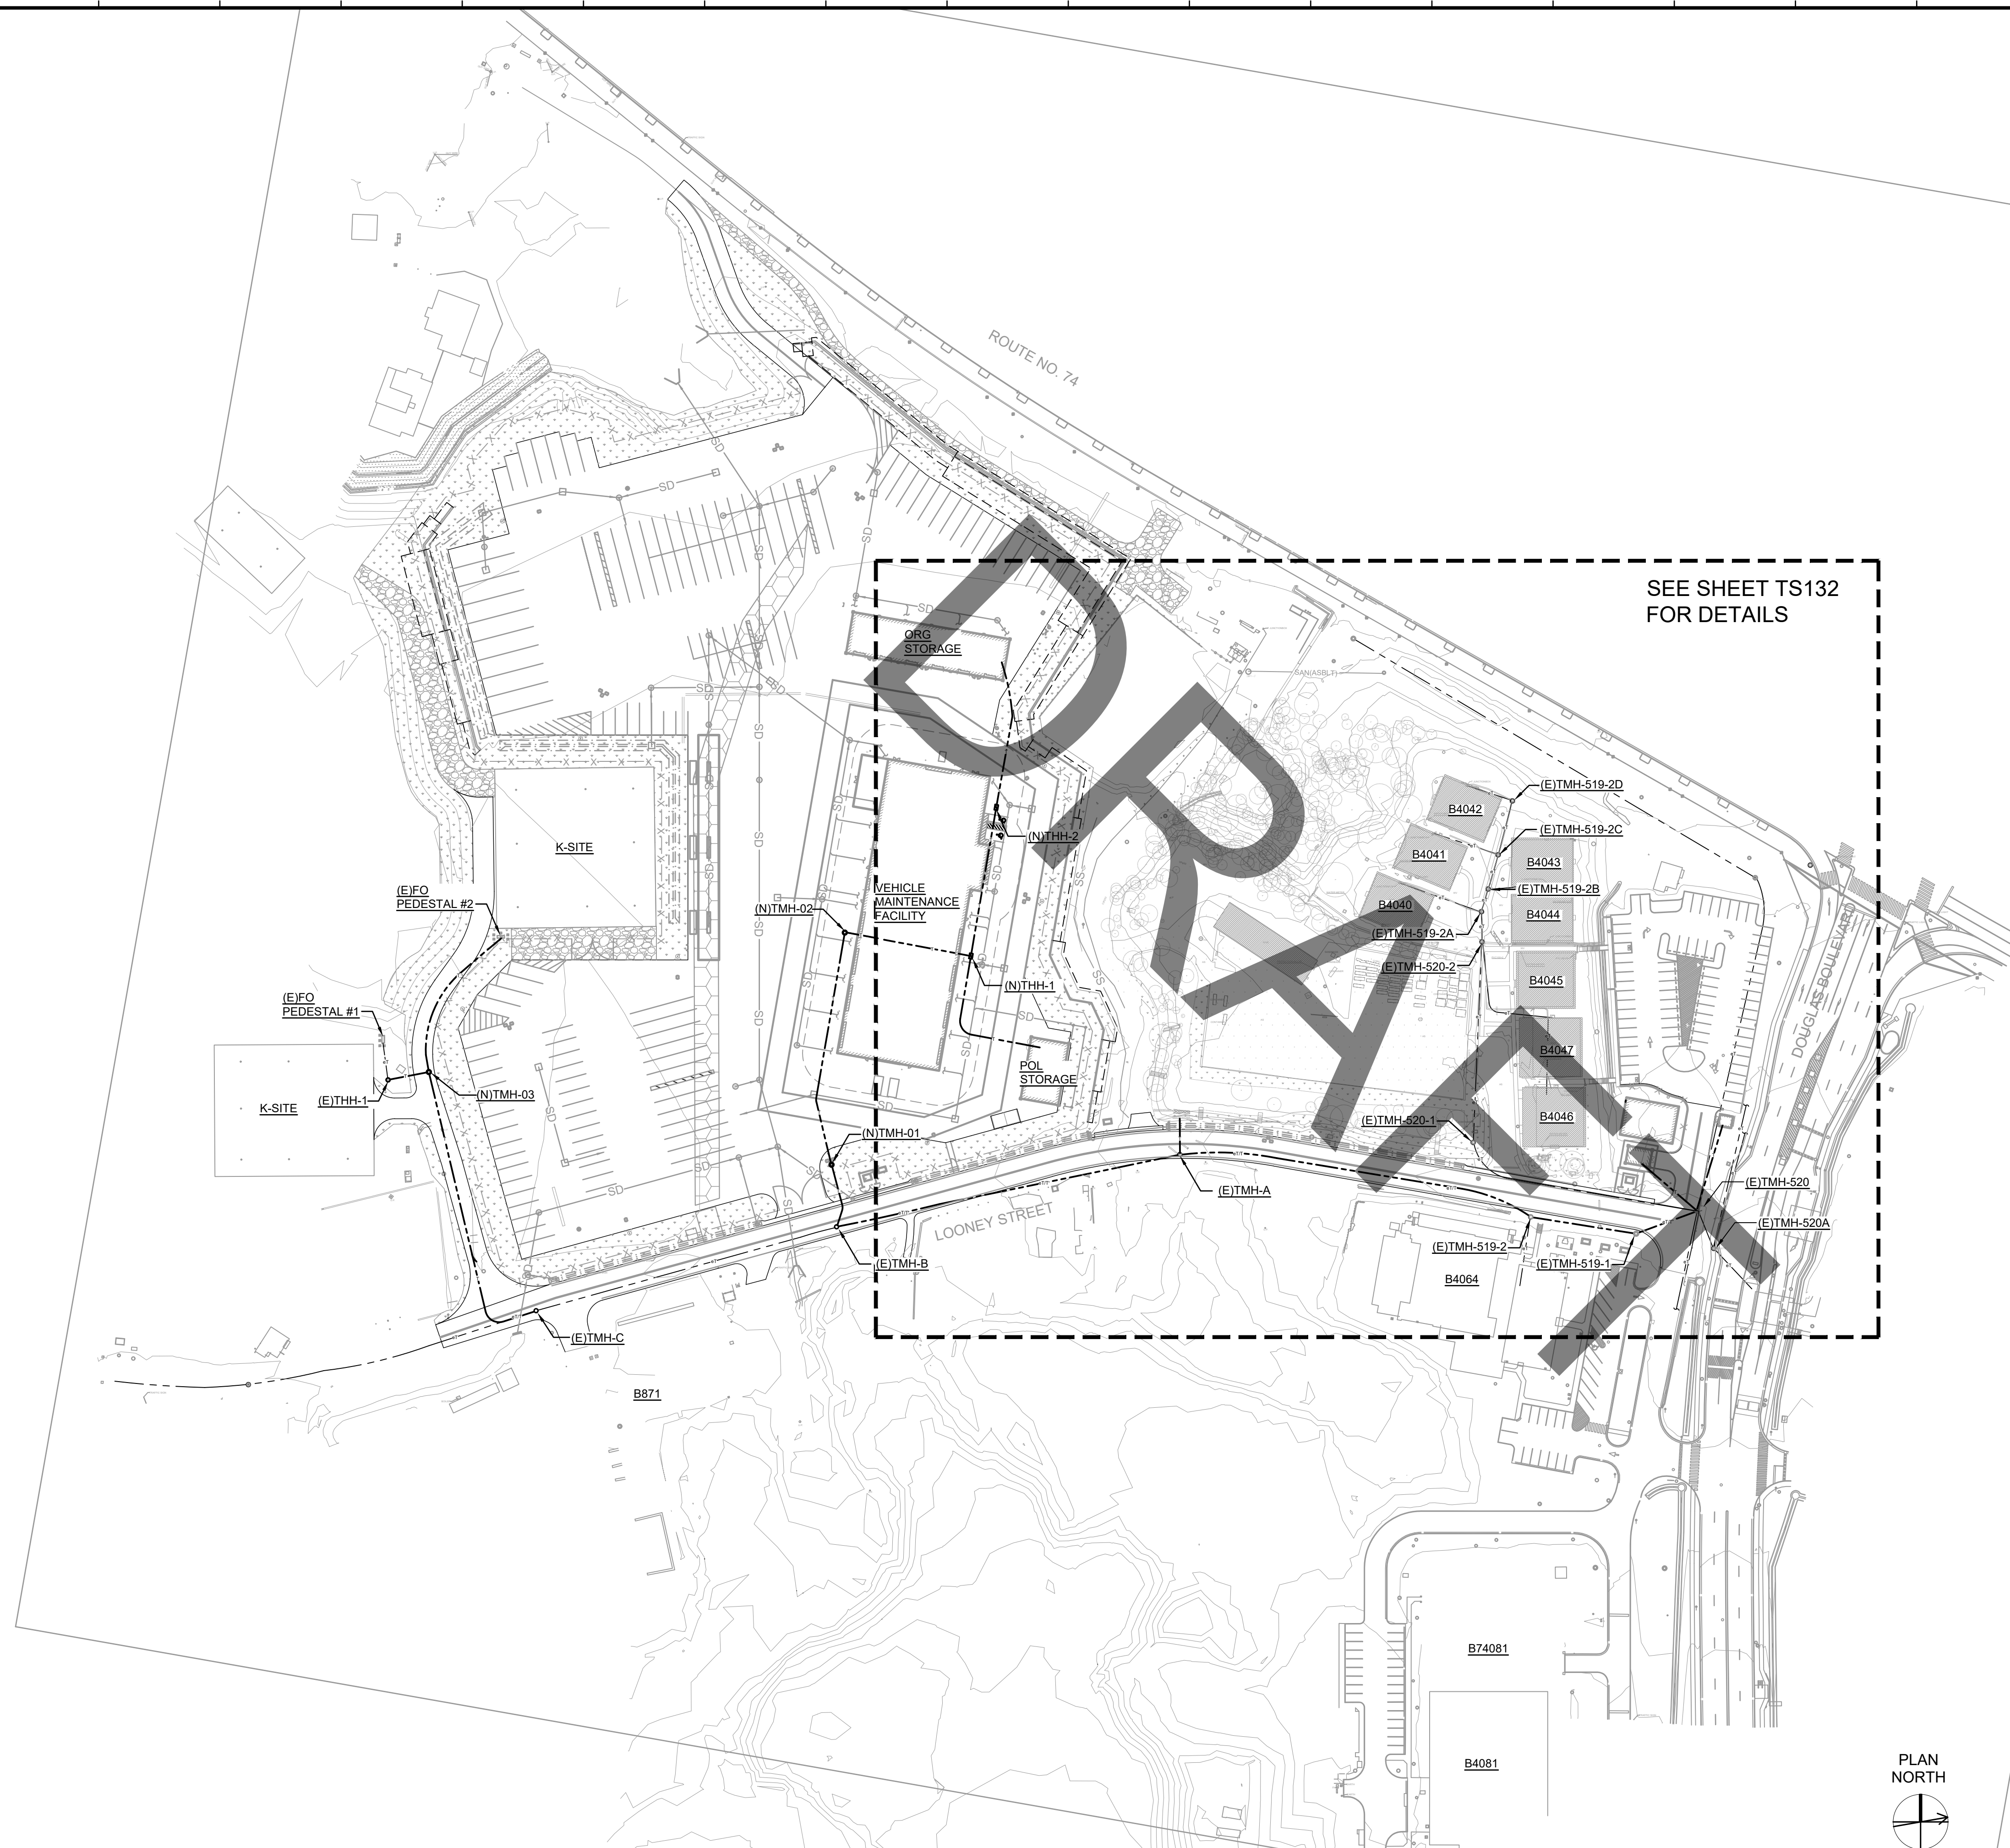

A1 OVERALL SITE TELECOMMUNICATION DEMOLITION PLAN (CLIN0004)
1:1000

GENERAL NOTES

1. SEE CIVIL AND ELECTRICAL PLANS FOR SITE DEMOLITION WORK AND CLOSELY COORDINATE THE DEMOLITION WORK FOR TELECOMMUNICATIONS SYSTEMS.
2. PRIOR TO ANY TELECOMMUNICATIONS INFRASTRUCTURE AND CABLE DEMOLITION WORK, ENSURE THAT THE NEW INFRASTRUCTURE AND CABLES ARE ESTABLISHED TO MINIMIZE DISRUPTION TO THE OPERATIONS OF THE EXISTING FACILITIES.
3. THE CONTRACTOR SHALL BE RESPONSIBLE TO SUBMIT A PROPOSED PHASING SCHEME IN COORDINATION WITH CIVIL AND ELECTRICAL WORK FOR REVIEW AND APPROVAL PRIOR TO START OF DEMOLITION WORK.

KEY NOTES

CLIN 0004

CLIN 0004

- CONSTRUCTION OF TEMPORARY FACILITIES AT SWING SPACE SITE MUST BE COMPLETED PRIOR TO DEMOLITION OF EXISTING ADA BUILDINGS (B4040 THRU B4047) AND SITE PREPARATION WORK FOR SSA FACILITIES.
- CONSTRUCTION OF NEW SUPPLY SUPPORT ACTIVITY (SSA) WAREHOUSE, STORAGE SHED AND ASSOCIATED TELECOMMUNICATIONS INFRASTRUCTURE.
- CONSTRUCTION OF SSA PARKING LOT.



US Army Corps
of Engineers®

[illegible]

US ARMY CORPS OF ENGINEERS JAPAN DISTRICT, OKINAWA AREA OFFICE USED-1, UNIT 35132 APO, 96344-5132	 SSFM INTERNATIONAL, INC. 501 SUMNER STREET, SUITE 620 HONOLULU, HAWAII 96817	UNCLASSIFIED BY: SOLICITATION NO.: DRAWN BY: CHECKED BY: SUBMITTED BY: SCALE: AS SHOWN CONTRACT NO.: FILE NAME: ISO A1	MODEL DATE: DATE:
--	---	---	----------------------

KADENA AIR BASE, OKINAWA, JAPAN
VEHICLE MAINTENANCE SHOP
FY20 MCA PN77833

SHEET ID
S131

INTERMEDIATE DESIGN