
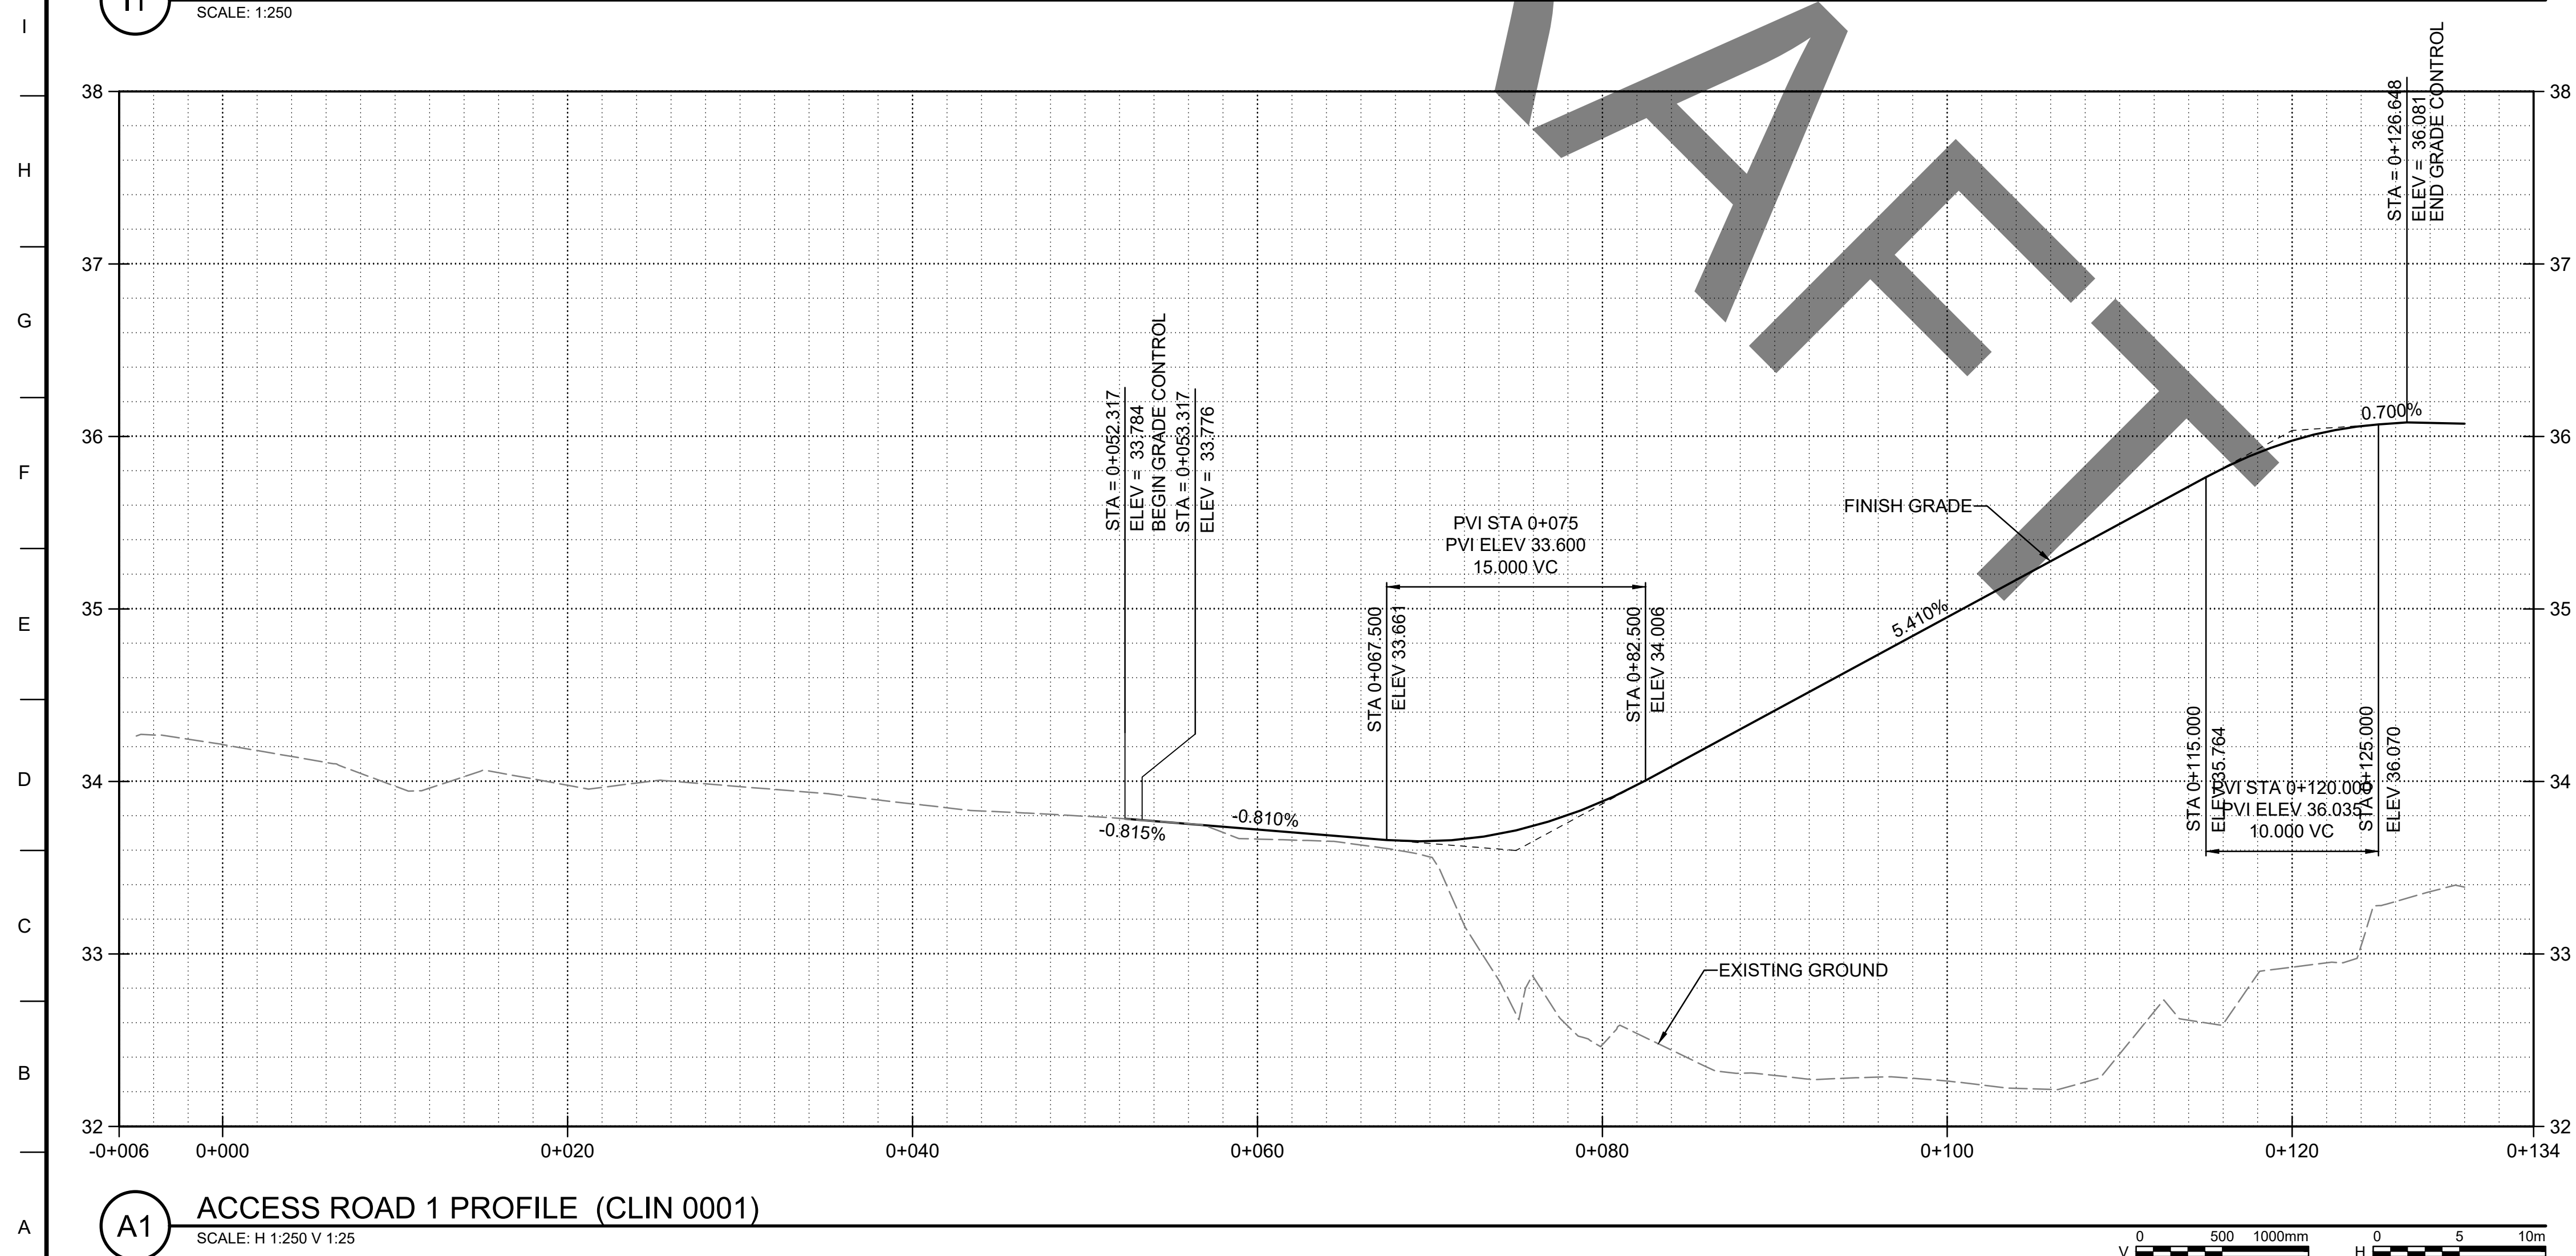


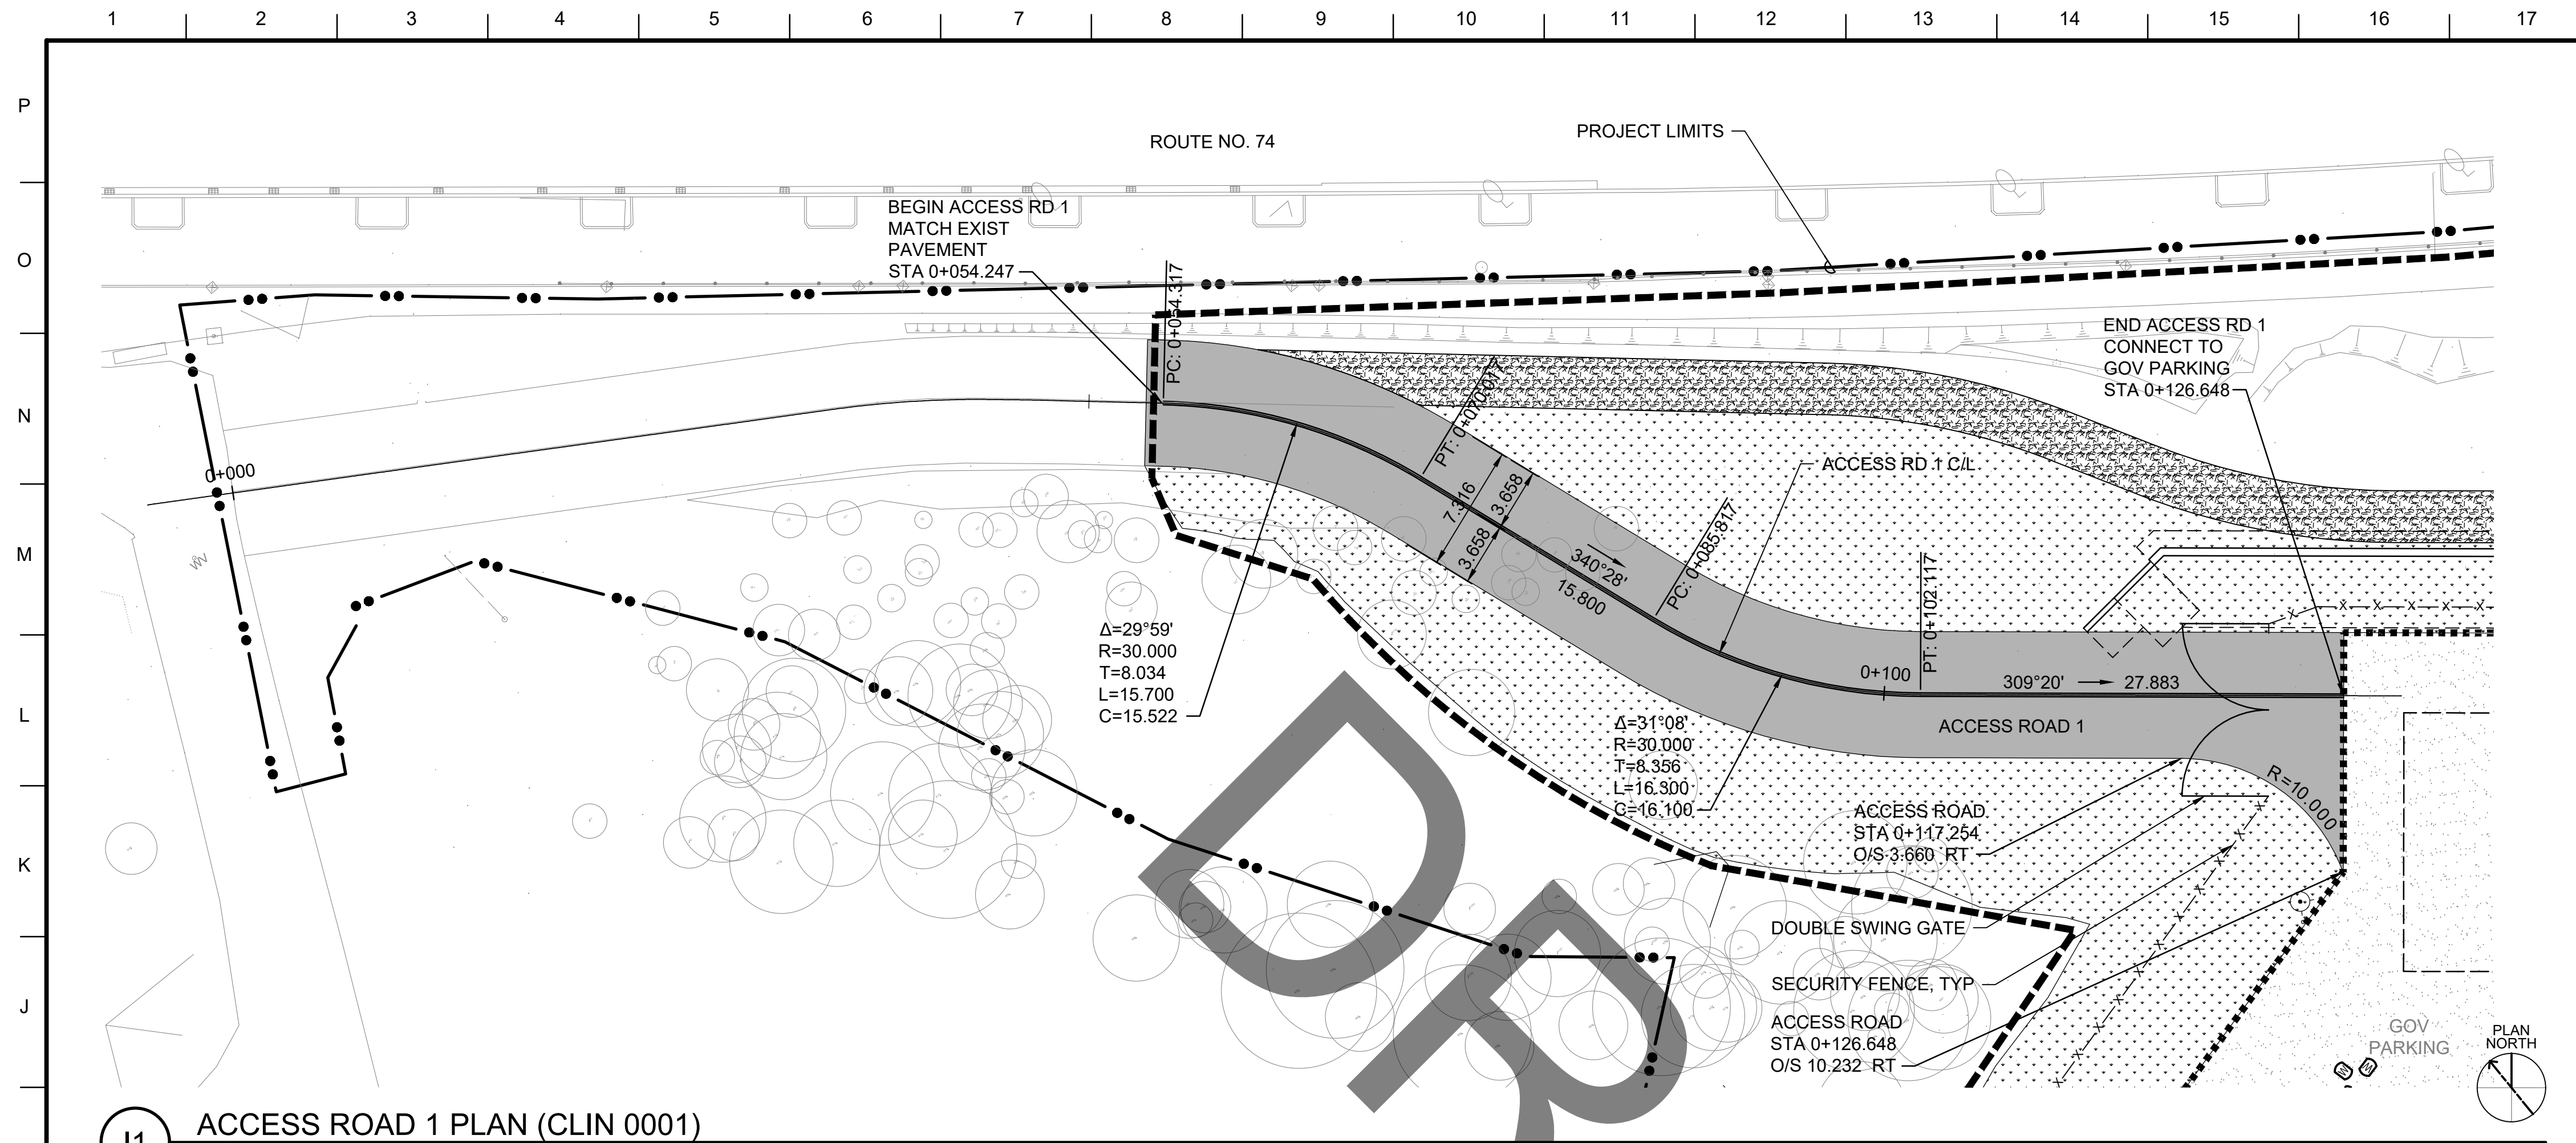

GENERAL NOTE

1. ALL DIMENSIONS SHOWN IN CALLOUT/NOTES ARE IN METERS UNLESS OTHERWISE NOTED.



SHEET LEGEND

- X-X-X-X-X- SECURITY FENCE
- RETAINING WALL
- PROJECT LIMITS
- AC PAVEMENT
- BUILDINGS
- PCC PAVEMENT
- GRAVEL
- SOD
- CONC ACCESS ROAD

CLIN 0001:
SITE PREPARATION, FENCING, AND
CLEARING VMS SITE.
VEHICLE MAINTENANCE SHOP.
LOONEY STREET WITH ALL UTILITIES.
PUMP HOUSE AND WATER STORAGE TANK.
PROVIDE ASPHALT CONCRETE PAVEMENT
IN ACCORDANCE WITH DETAIL M10/CP501.

CLIN 0001

KEY PLAN

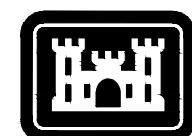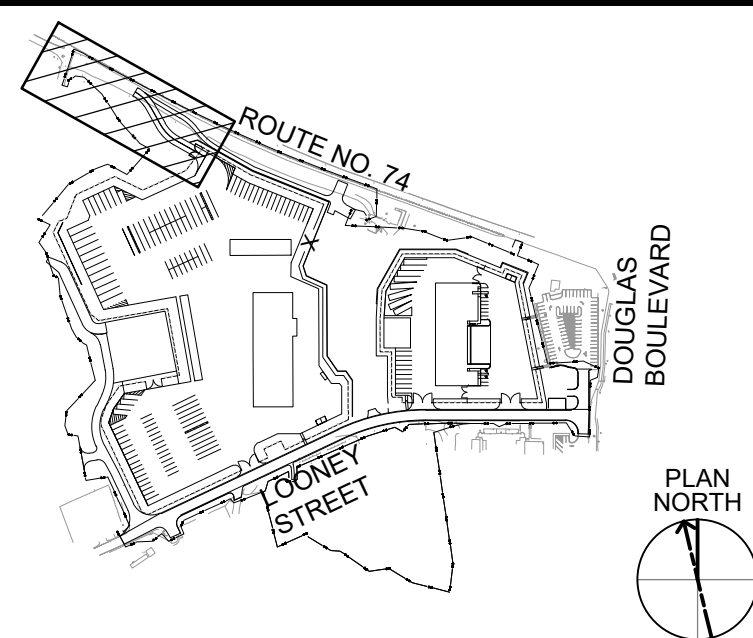

US Army Corps
of Engineers®

ISSUE DATE:
DESIGNED BY:
DRAWN BY:
CHECKED BY:
SUBMITTED BY:
SIZE: ISO A1
FILE NAME:

SOLICITATION NO.:
CONTRACT NO.:
SCALE:
AS SHOWN

US ARMY CORPS OF ENGINEERS
JAPAN DISTRICT, OKINAWA AREA OFFICE
USAE-J UNIT 35132
APO, AP 96374-5132


SSEM INTERNATIONAL, INC.
501 SUMNER STREET, SUITE 620
HONOLULU, HAWAII 96817

KADENA AIR BASE, OKINAWA, JAPAN
VEHICLE MAINTENANCE SHOP
FY20 MCA PN77833


ACCESS ROAD PLAN AND PROFILE

SHEET ID
CP104

INTERMEDIATE DESIGN

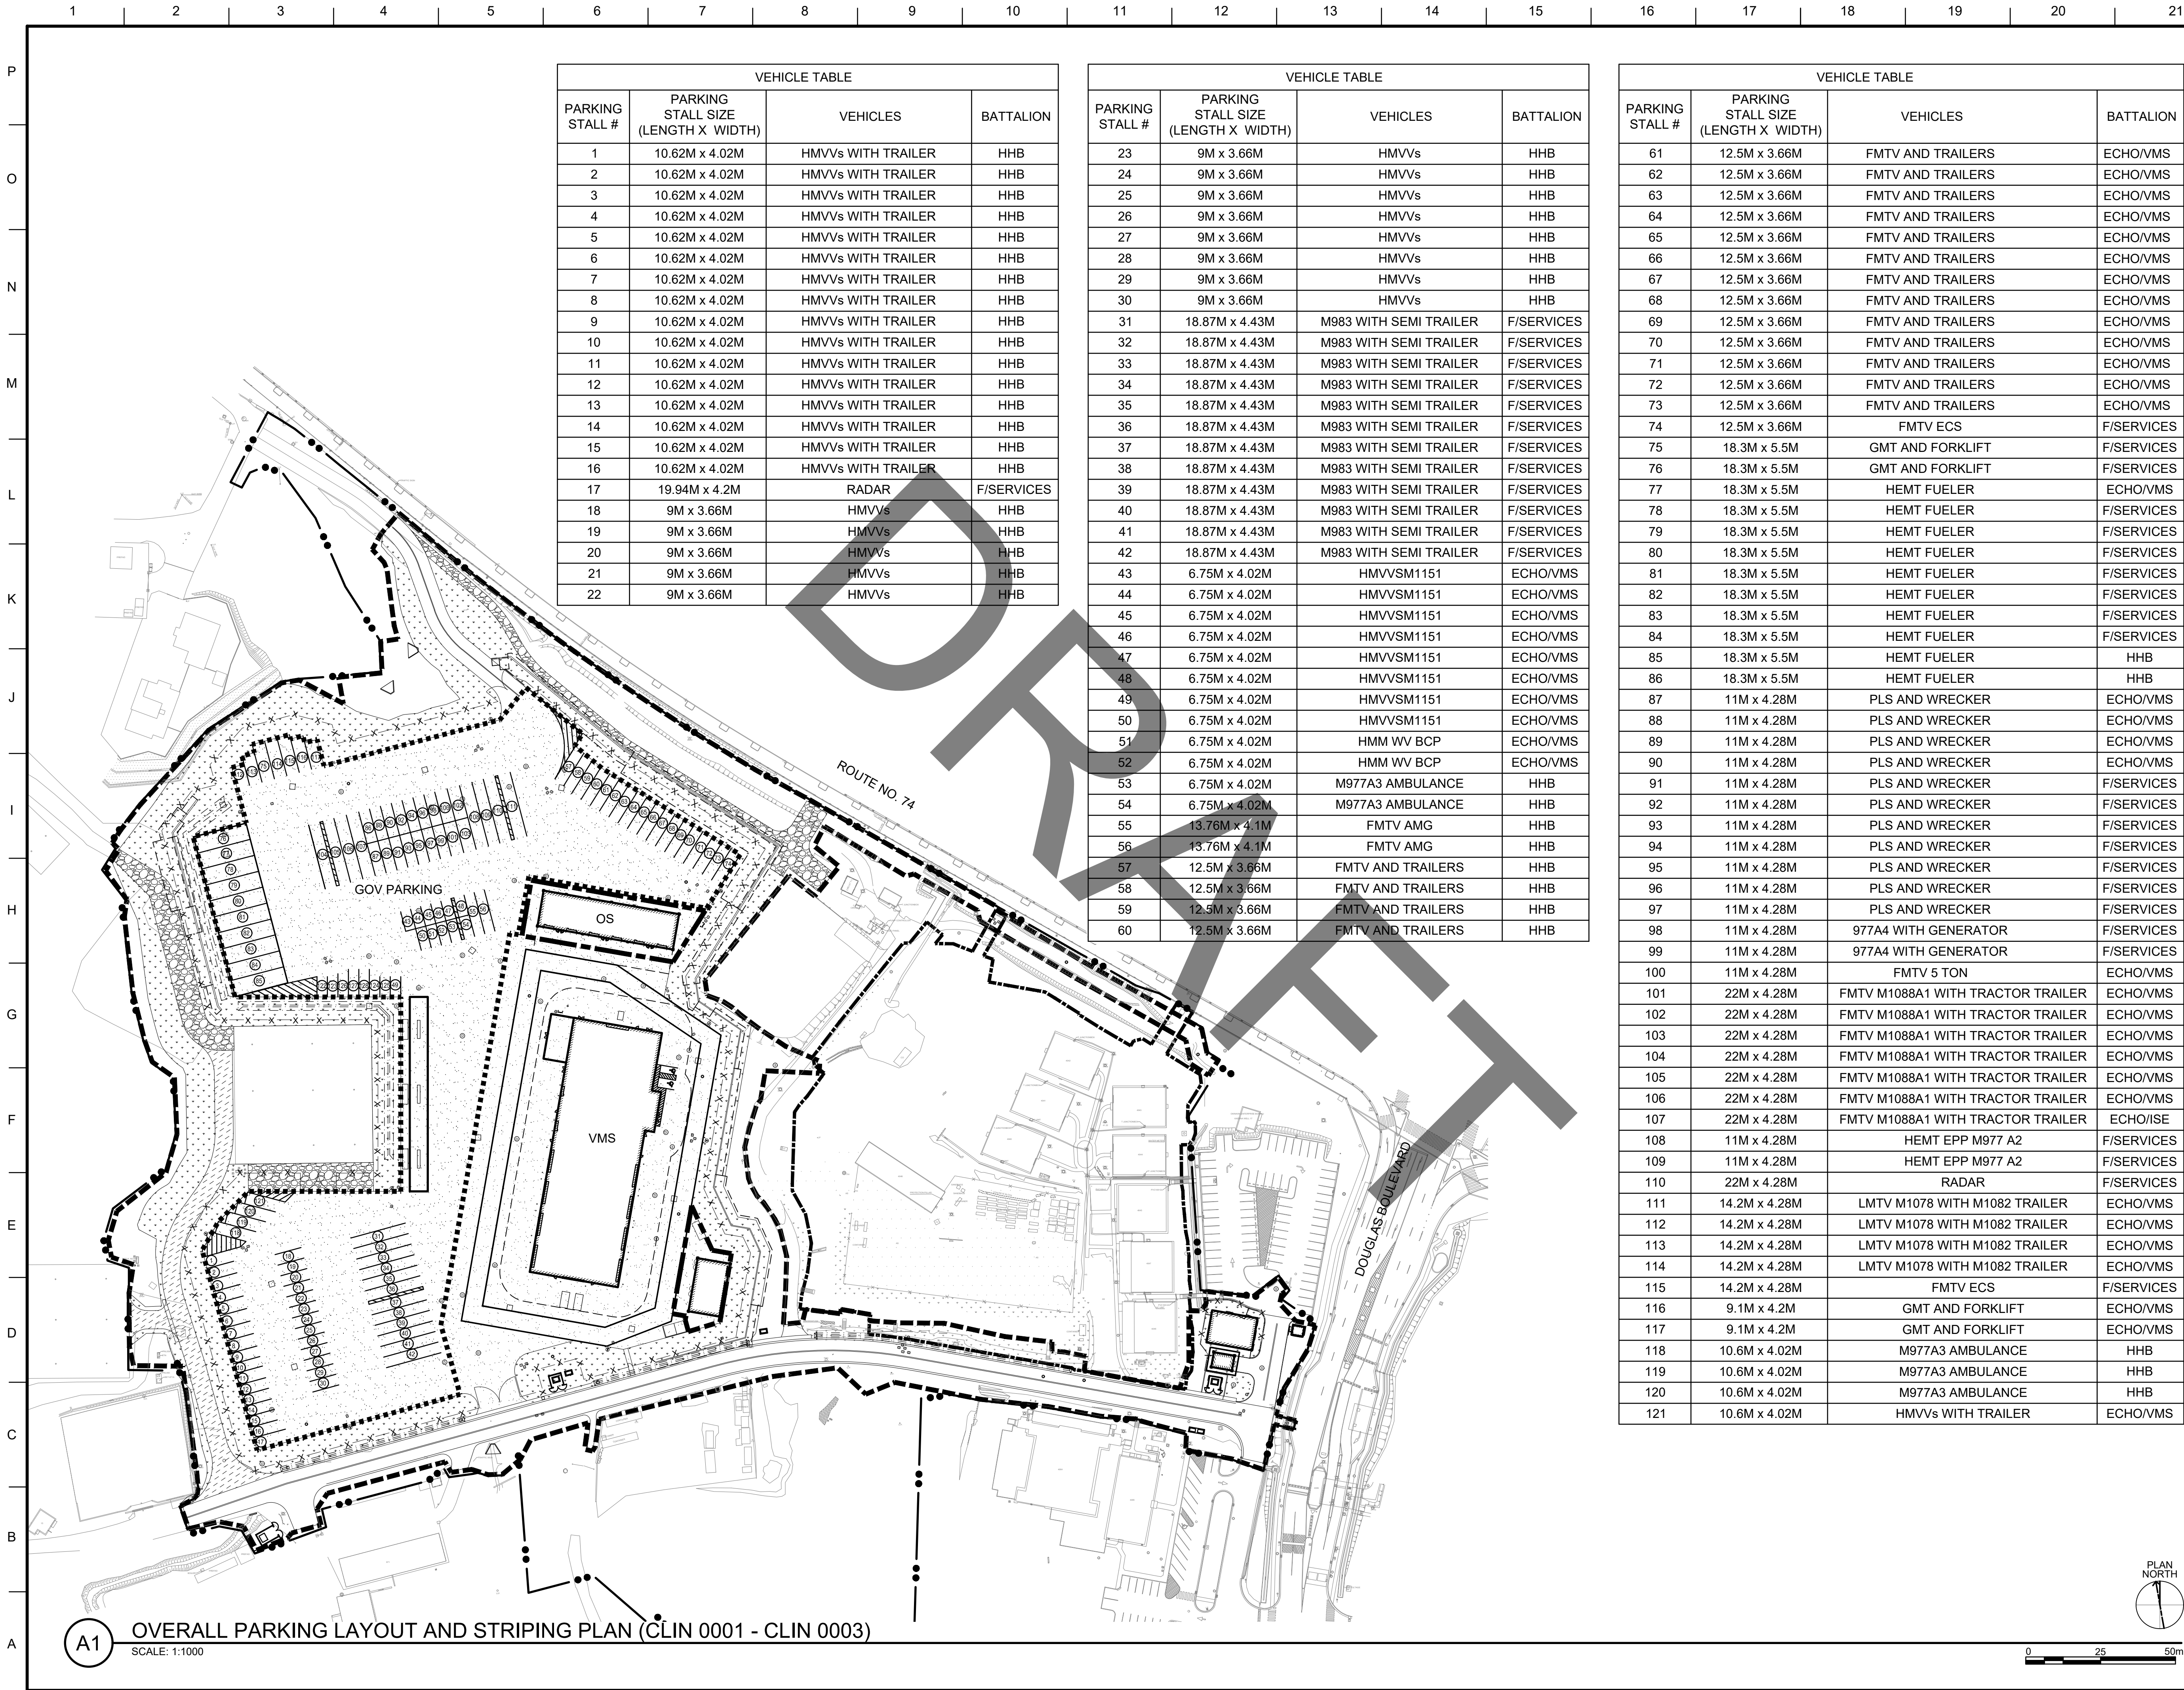

A1 OVERALL PARKING LAYOUT AND STRIPING PLAN (CLIN 0001 - CLIN 0003)
SCALE: 1:1000

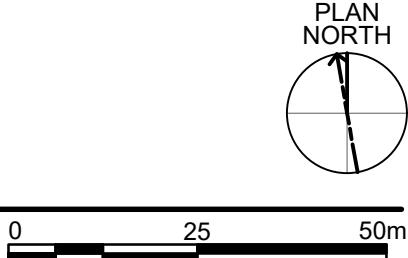

US Army Corps of Engineers®

DESIGNED BY:		ISSUE DATE:	
DRAWN BY:		SOLICITATION NO.:	
CHECKED BY:		CONTRACT NO.:	
SUBMITTED BY:		SCALE:	
SIZE:		AS SHOWN	
FILE NAME:		MARK	
DATE		DESCRIPTION	

US ARMY CORPS OF ENGINEERS
JAPAN DISTRICT, OKINAWA AREA OFFICE
USAFED-J UNIT 35132
APO, AP 96374-5132

SSFM INTERNATIONAL, INC.
501 SUMNER STREET, SUITE 620
HONOLULU, HAWAII 96817


KADANA AIR BASE, OKINAWA, JAPAN
VEHICLE MAINTENANCE SHOP
FY20 MCA PN77833

OVERALL PARKING LAYOUT AND STRIPING PLAN (CLIN 0001 - CLIN 0003)

SHEET ID

CP121

INTERMEDIATE DESIGN

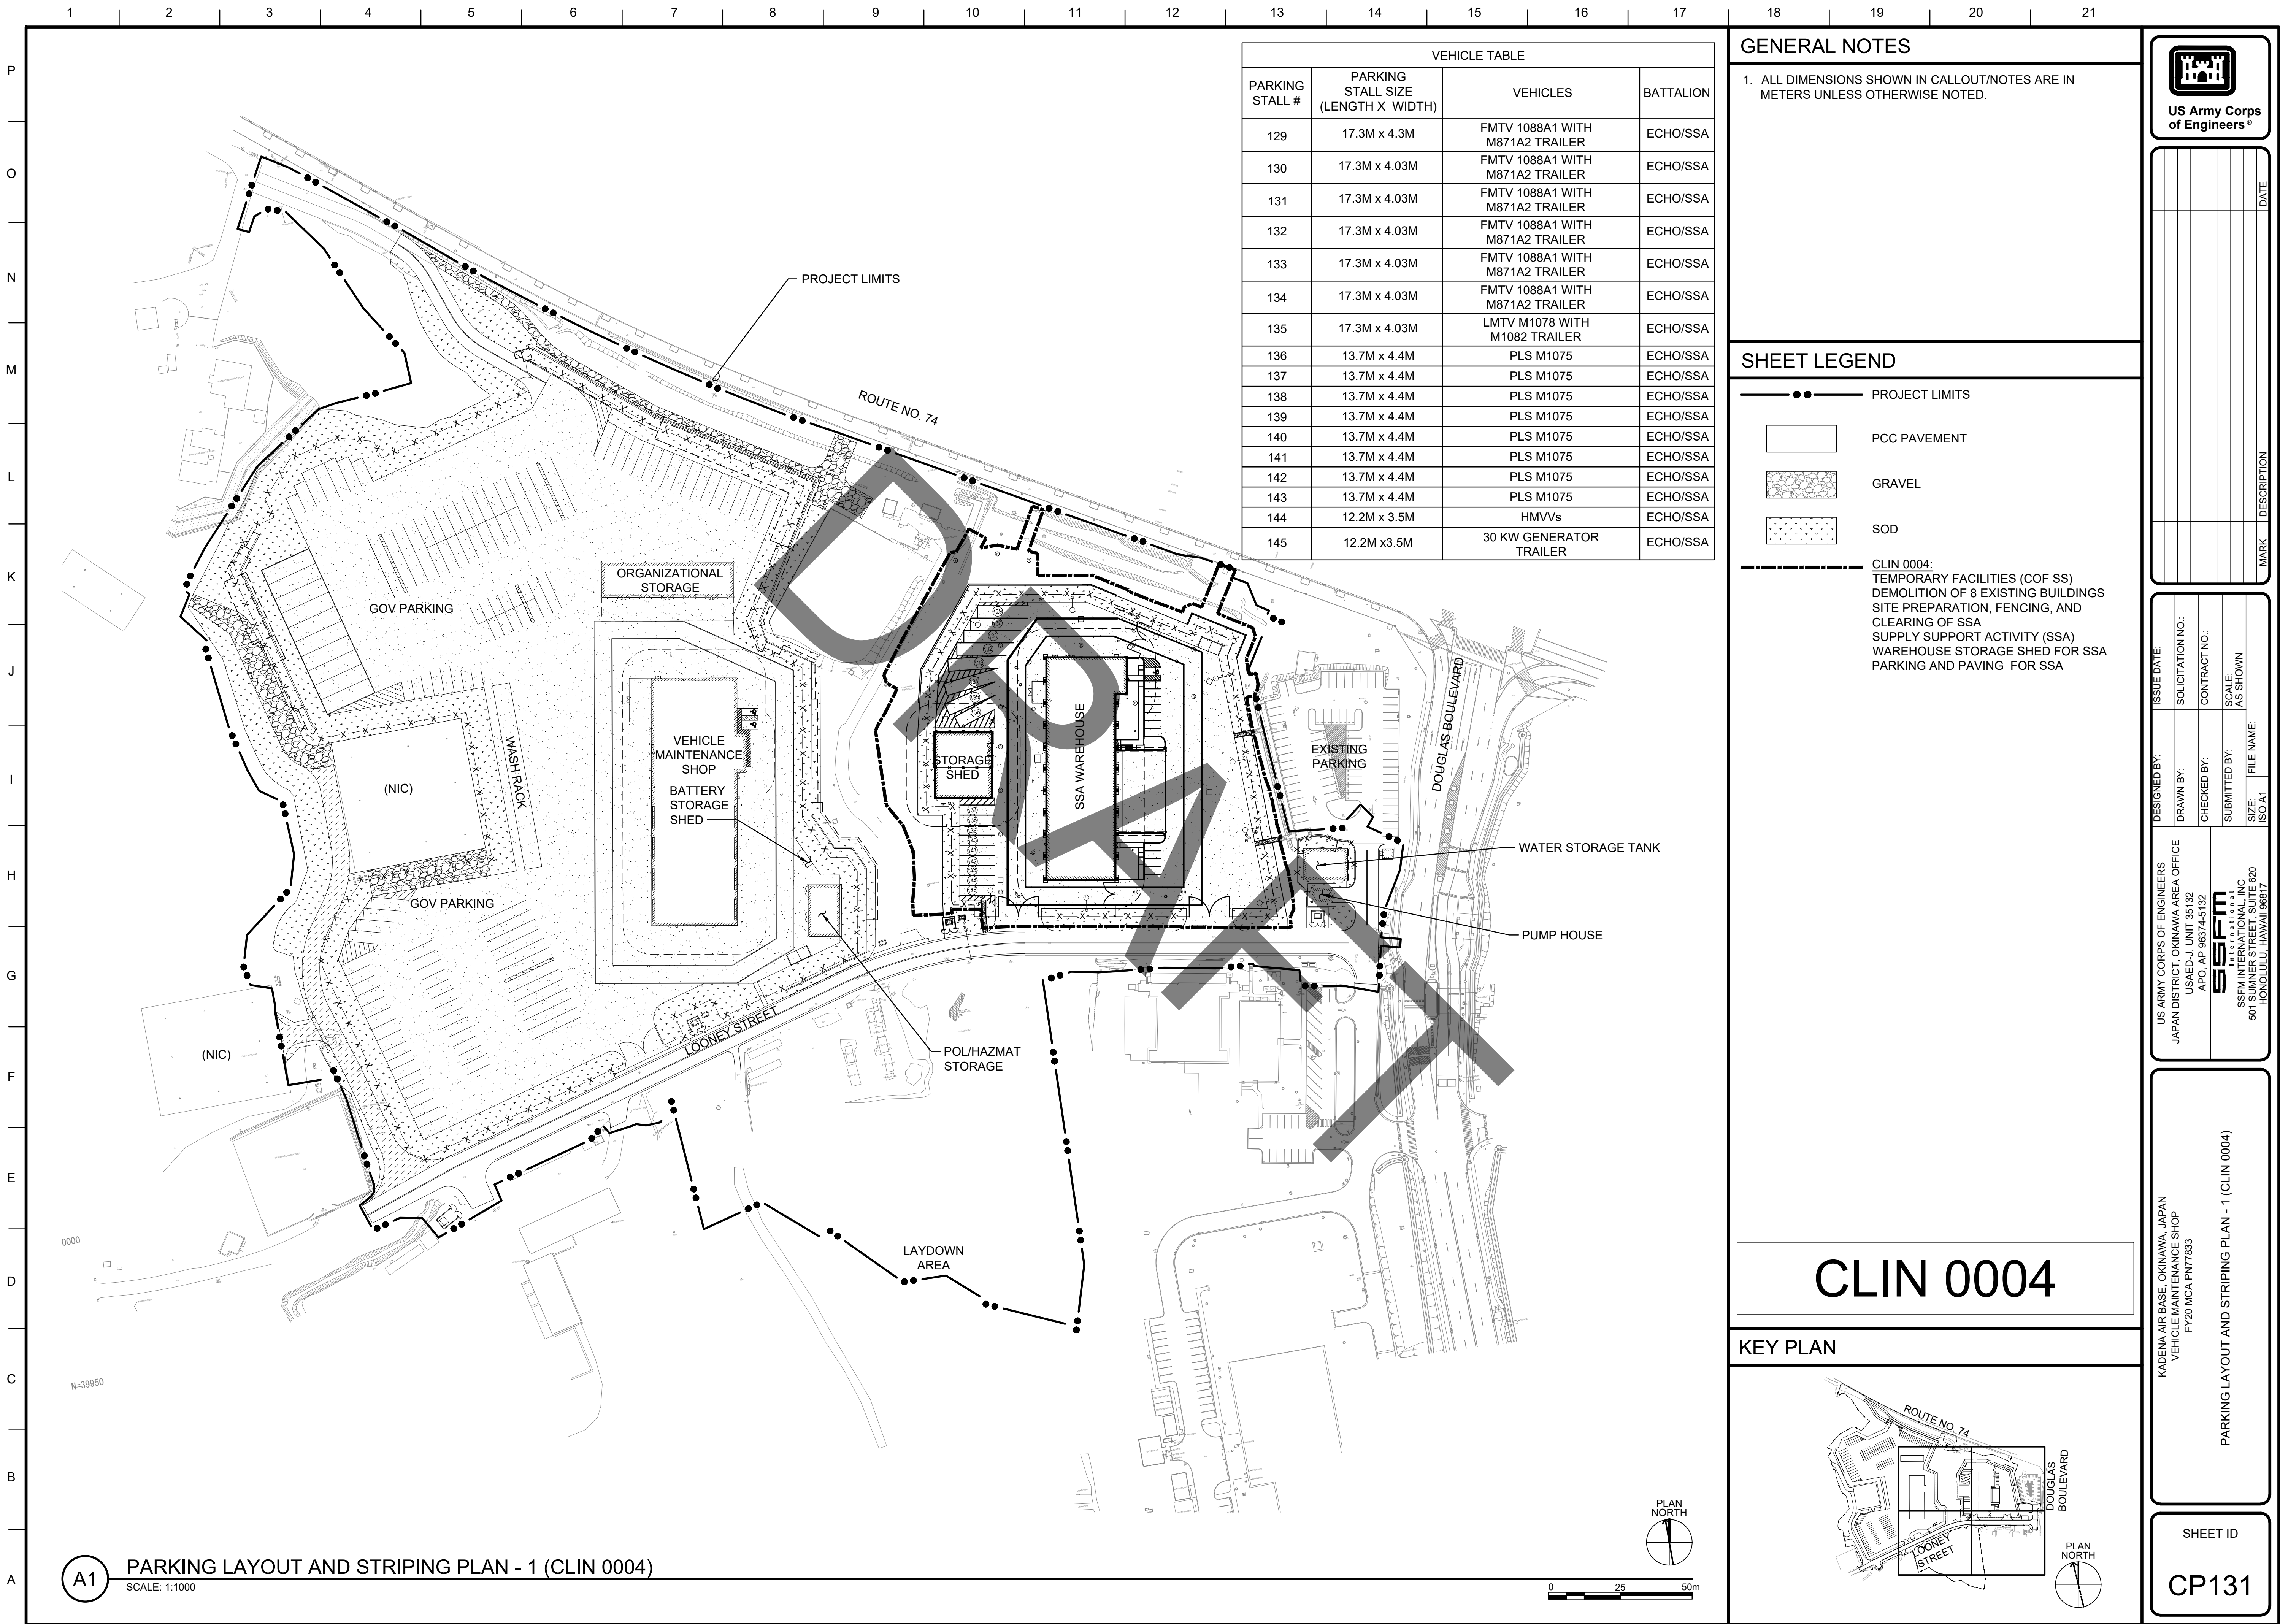

VEHICLE TABLE			
PARKING STALL #	PARKING STALL SIZE (LENGTH X WIDTH)	VEHICLES	BATTALION
129	17.3M x 4.3M	FMTV 1088A1 WITH M871A2 TRAILER	ECHO/SSA
130	17.3M x 4.03M	FMTV 1088A1 WITH M871A2 TRAILER	ECHO/SSA
131	17.3M x 4.03M	FMTV 1088A1 WITH M871A2 TRAILER	ECHO/SSA
132	17.3M x 4.03M	FMTV 1088A1 WITH M871A2 TRAILER	ECHO/SSA
133	17.3M x 4.03M	FMTV 1088A1 WITH M871A2 TRAILER	ECHO/SSA
134	17.3M x 4.03M	FMTV 1088A1 WITH M871A2 TRAILER	ECHO/SSA
135	17.3M x 4.03M	LMTV M1078 WITH M1082 TRAILER	ECHO/SSA
136	13.7M x 4.4M	PLS M1075	ECHO/SSA
137	13.7M x 4.4M	PLS M1075	ECHO/SSA
138	13.7M x 4.4M	PLS M1075	ECHO/SSA
139	13.7M x 4.4M	PLS M1075	ECHO/SSA
140	13.7M x 4.4M	PLS M1075	ECHO/SSA
141	13.7M x 4.4M	PLS M1075	ECHO/SSA
142	13.7M x 4.4M	PLS M1075	ECHO/SSA
143	13.7M x 4.4M	PLS M1075	ECHO/SSA
144	12.2M x 3.5M	HMVVs	ECHO/SSA
145	12.2M x3.5M	30 KW GENERATOR TRAILER	ECHO/SSA

GENERAL NOTES

1. ALL DIMENSIONS SHOWN IN CALLOUT/NOTES ARE IN METERS UNLESS OTHERWISE NOTED.

SHEET LEGEND

PROJECT LIMITS

PCC PAVEMENT

GRAVEL

SOD

CLIN 0004:
TEMPORARY FACILITIES (COF SS)
DEMOLITION OF 8 EXISTING BUILDINGS
SITE PREPARATION, FENCING, AND
CLEARING OF SSA
SUPPLY SUPPORT ACTIVITY (SSA)
WAREHOUSE STORAGE SHED FOR SSA
PARKING AND PAVING FOR SSA

DESIGNED BY:	ISSUE DATE:
DRAWN BY:	SOLICITATION NO.:
CHECKED BY:	CONTRACT NO.:
SUBMITTED BY:	SCALE:
SIZE:	AS SHOWN
FILE NAME:	
ISO A1	
US ARMY CORPS OF ENGINEERS JAPAN DISTRICT, OKINAWA AREA OFFICE USAD-J, UNIT 35132 APO, AP 96374-5132	
 SSFM INTERNATIONAL, INC. 501 SUMNER STREET, SUITE 620 HONOLULU, HAWAII 96817	

CLIN 0004


KEY PLAN

KADENA AIR BASE, OKINAWA, JAPAN
VEHICLE MAINTENANCE SHOP
FY20 MCA PN77833

PARKING LAYOUT AND STRIPING PLAN - 1 (CLIN 0004)

SHEET ID
CP131

INTERMEDIATE DESIGN

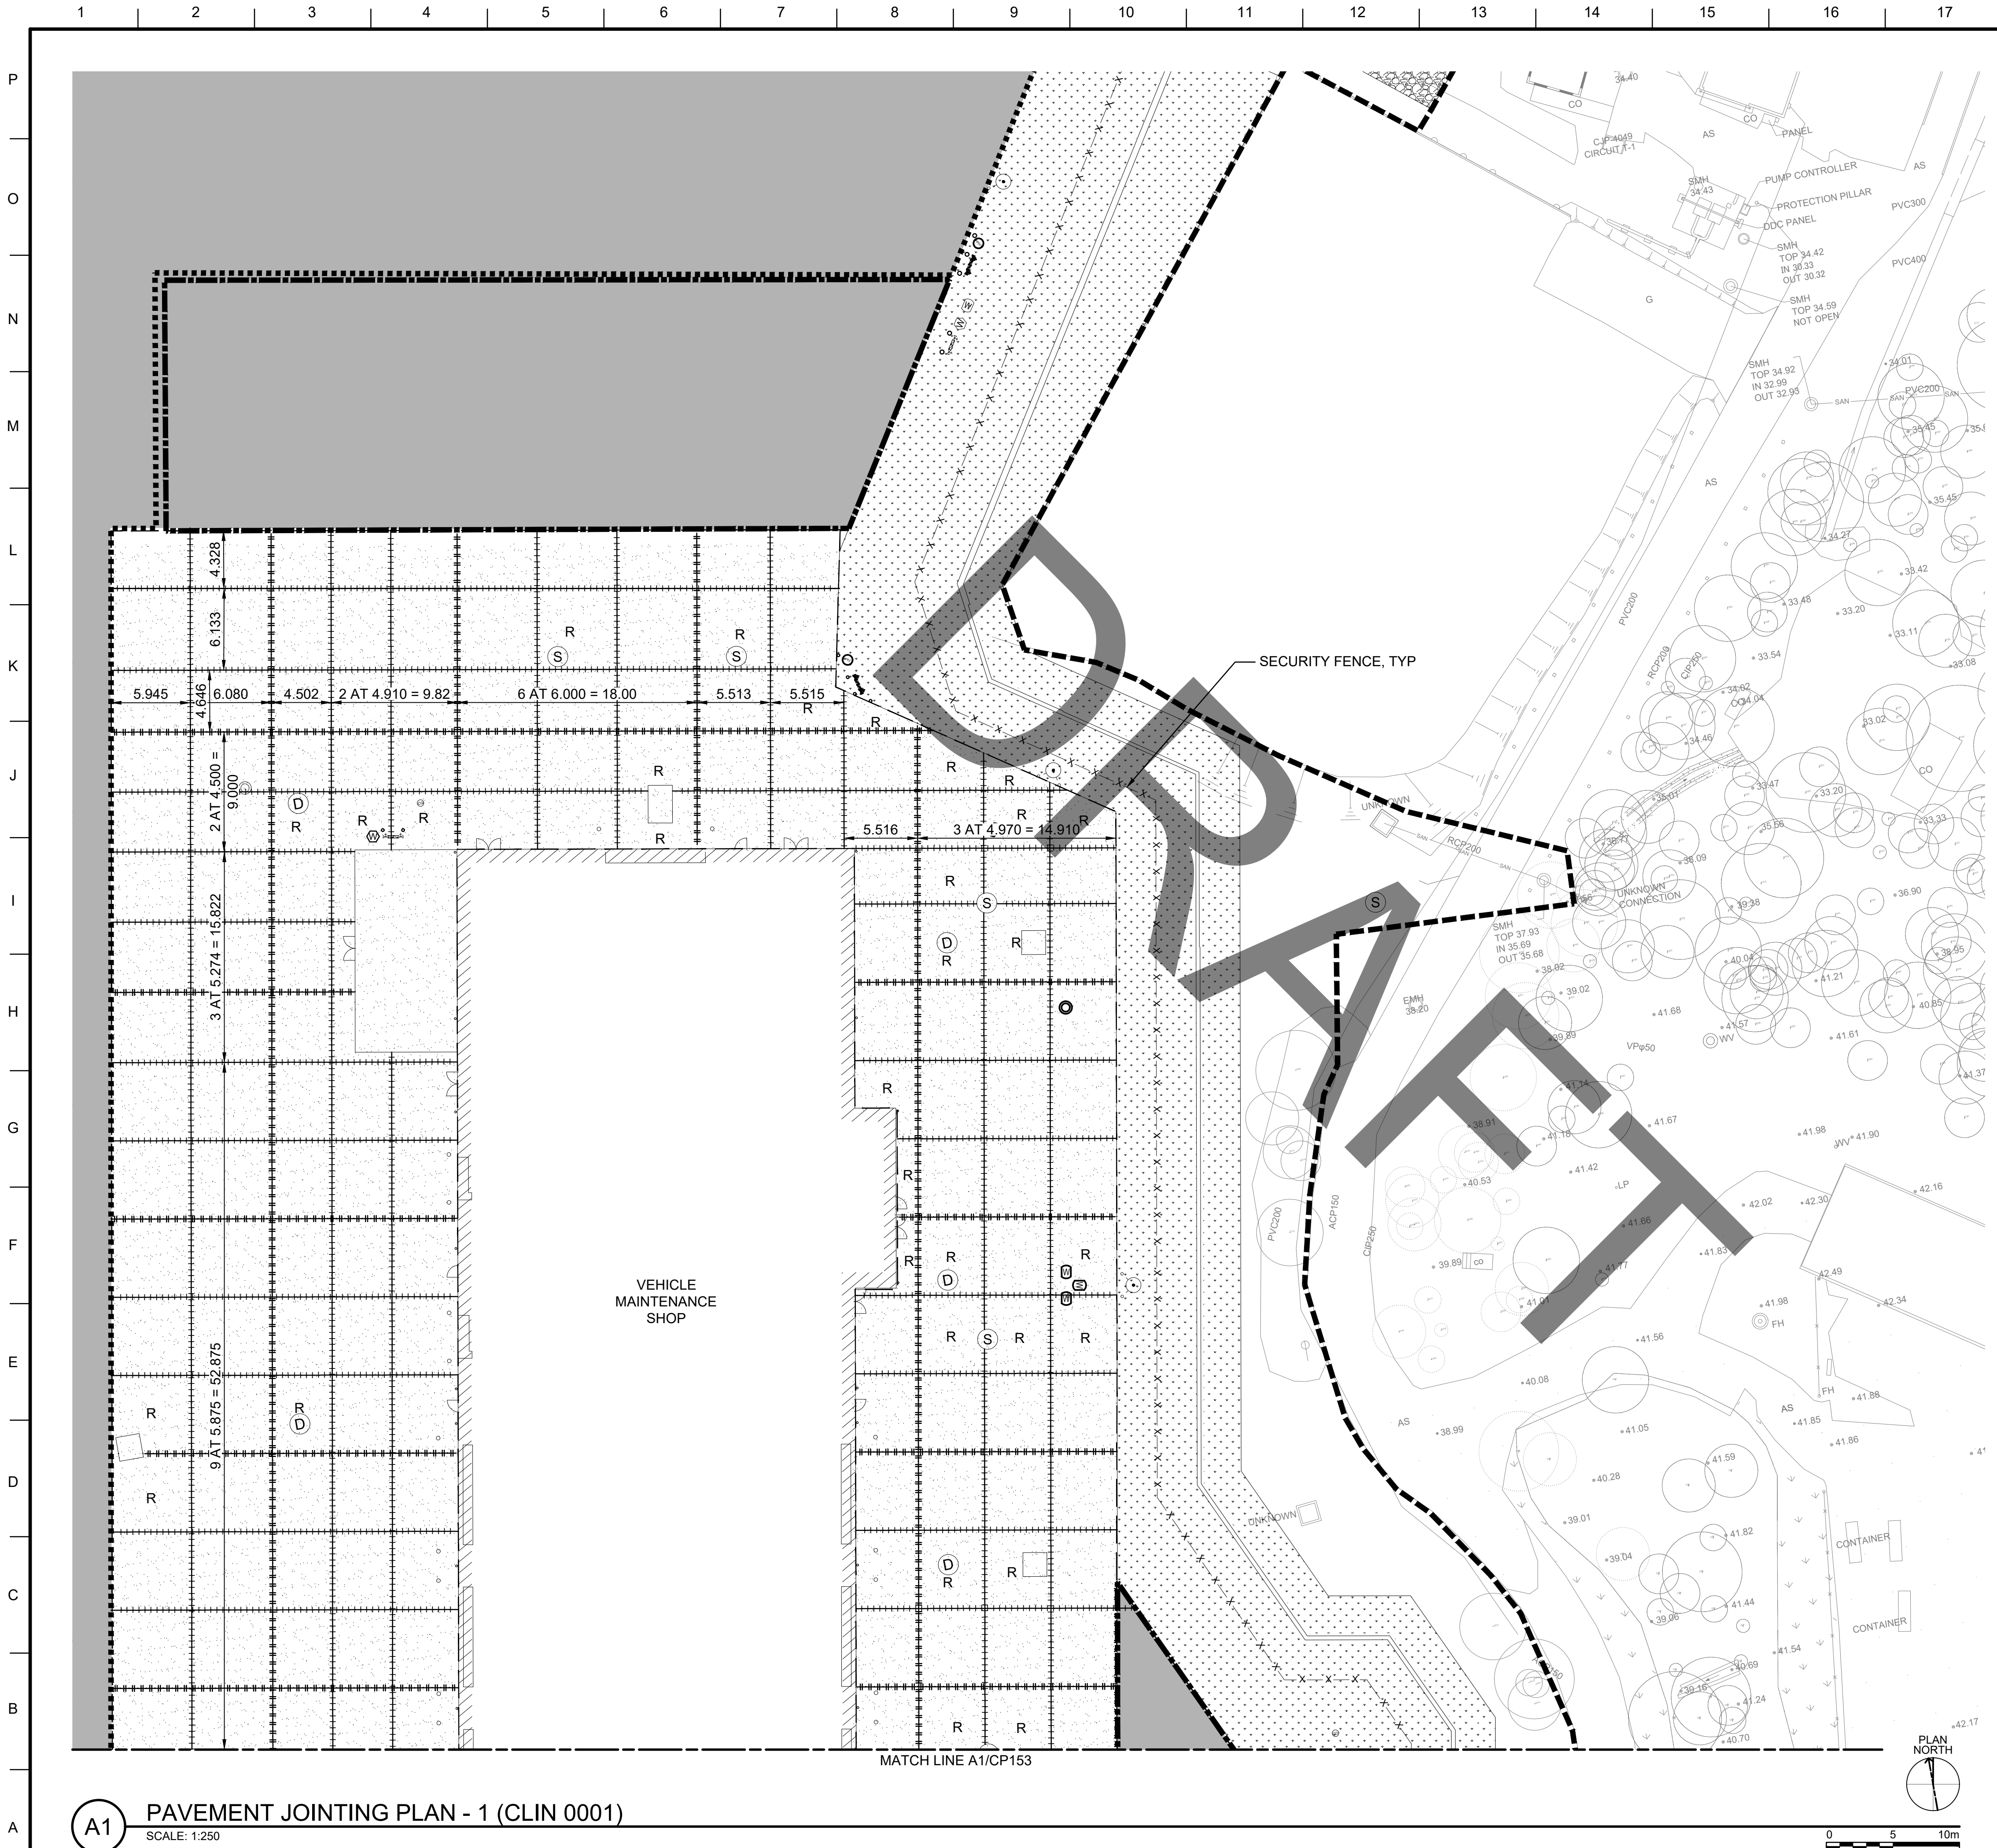

A1 PAVEMENT JOINTING PLAN - 1 (CLIN 0001)
SCALE: 1:250

GENERAL NOTES


- ALL DIMENSIONS SHOWN IN CALLOUT/NOTES ARE IN METERS UNLESS OTHERWISE NOTED.
- REMOVE ALL EXISTING TREES WITHIN PROJECT LIMITS UNLESS OTHERWISE NOTED.
- ALL TREES OF SIGNIFICANCE, SUCH AS LARGE BANYAN TREES, MUST BE REPORTED TO THE NATURAL RESOURCE MANAGER, KADENA AIR BASE.
- A TREE COMPENSATION SURVEY WILL BE CONDUCTED BY THE OKINAWA DEFENSE BUREAU (ODB) FOR LAND LEASED FROM A LOCAL OWNER. COORDINATE THE ODB SURVEY PRIOR TO CONSTRUCTION.
- SEE ELECTRICAL AND COMMUNICATION PLANS FOR ELEC/COMM DEMOLITION.

SHEET LEGEND

- PROJECT LIMITS
- AC PAVEMENT
- BUILDINGS
- PCC PAVEMENT
- DOWELED JOINTS
- LONGITUDINAL CONSTRUCTION JOINTS
- TRANVERSE CONSTRUCTION JOINTS
- SPECIAL REINFORCING, SEE JOINTING CRITERIA NOTES
- CLIN 0001:
SITE PREPARATION, FENCING, AND CLEARING VMS SITE.
VEHICLE MAINTENANCE SHOP BUILDING
LOONEY STREET WITH ALL UTILITIES.
PUMP HOUSE AND WATER STORAGE TANK.
PROVIDE ASPHALT CONCRETE PAVEMENT AND PCC PAVEMENT IN ACCORDANCE WITH DETAIL. M10 CP501 H7 CP501

CLIN 0001

KEY PLAN

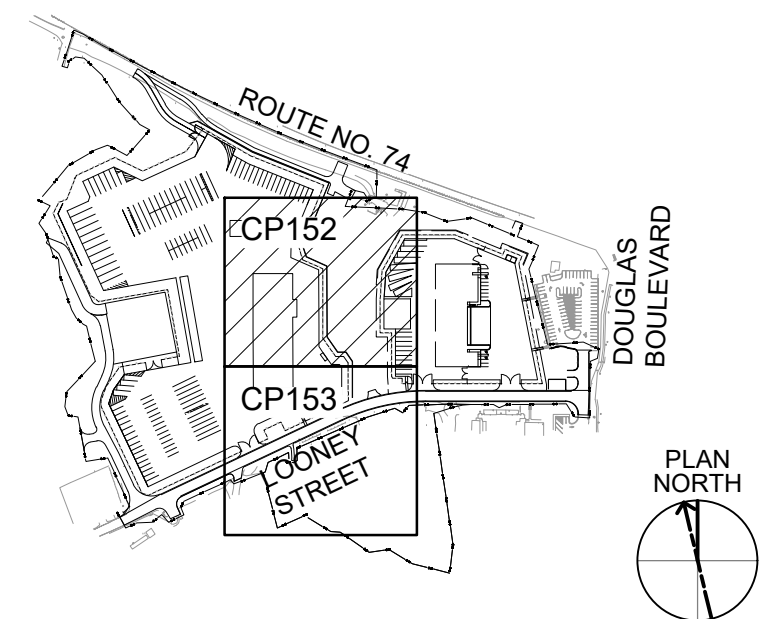

US Army Corps of Engineers®

ISSUE DATE:		SOLICITATION NO.:		CONTRACT NO.:	
DESIGNED BY:	DRAWN BY:	CHECKED BY:	SUBMITTED BY:	SCALE:	AS SHOWN
US ARMY CORPS OF ENGINEERS JAPAN DISTRICT, OKINAWA AREA OFFICE USAED-J, UNIT 35132 APO, AP 96374-5132			SSFM INTERNATIONAL, INC. 501 SUMNER STREET, SUITE 620 HONOLULU, HAWAII 96817		


KADENA AIR BASE, OKINAWA, JAPAN
VEHICLE MAINTENANCE SHOP
FY20 MCA PN77833

PAVEMENT JOINTING PLAN - 1 (CLIN 0001)

SHEET ID

CP152

INTERMEDIATE DESIGN

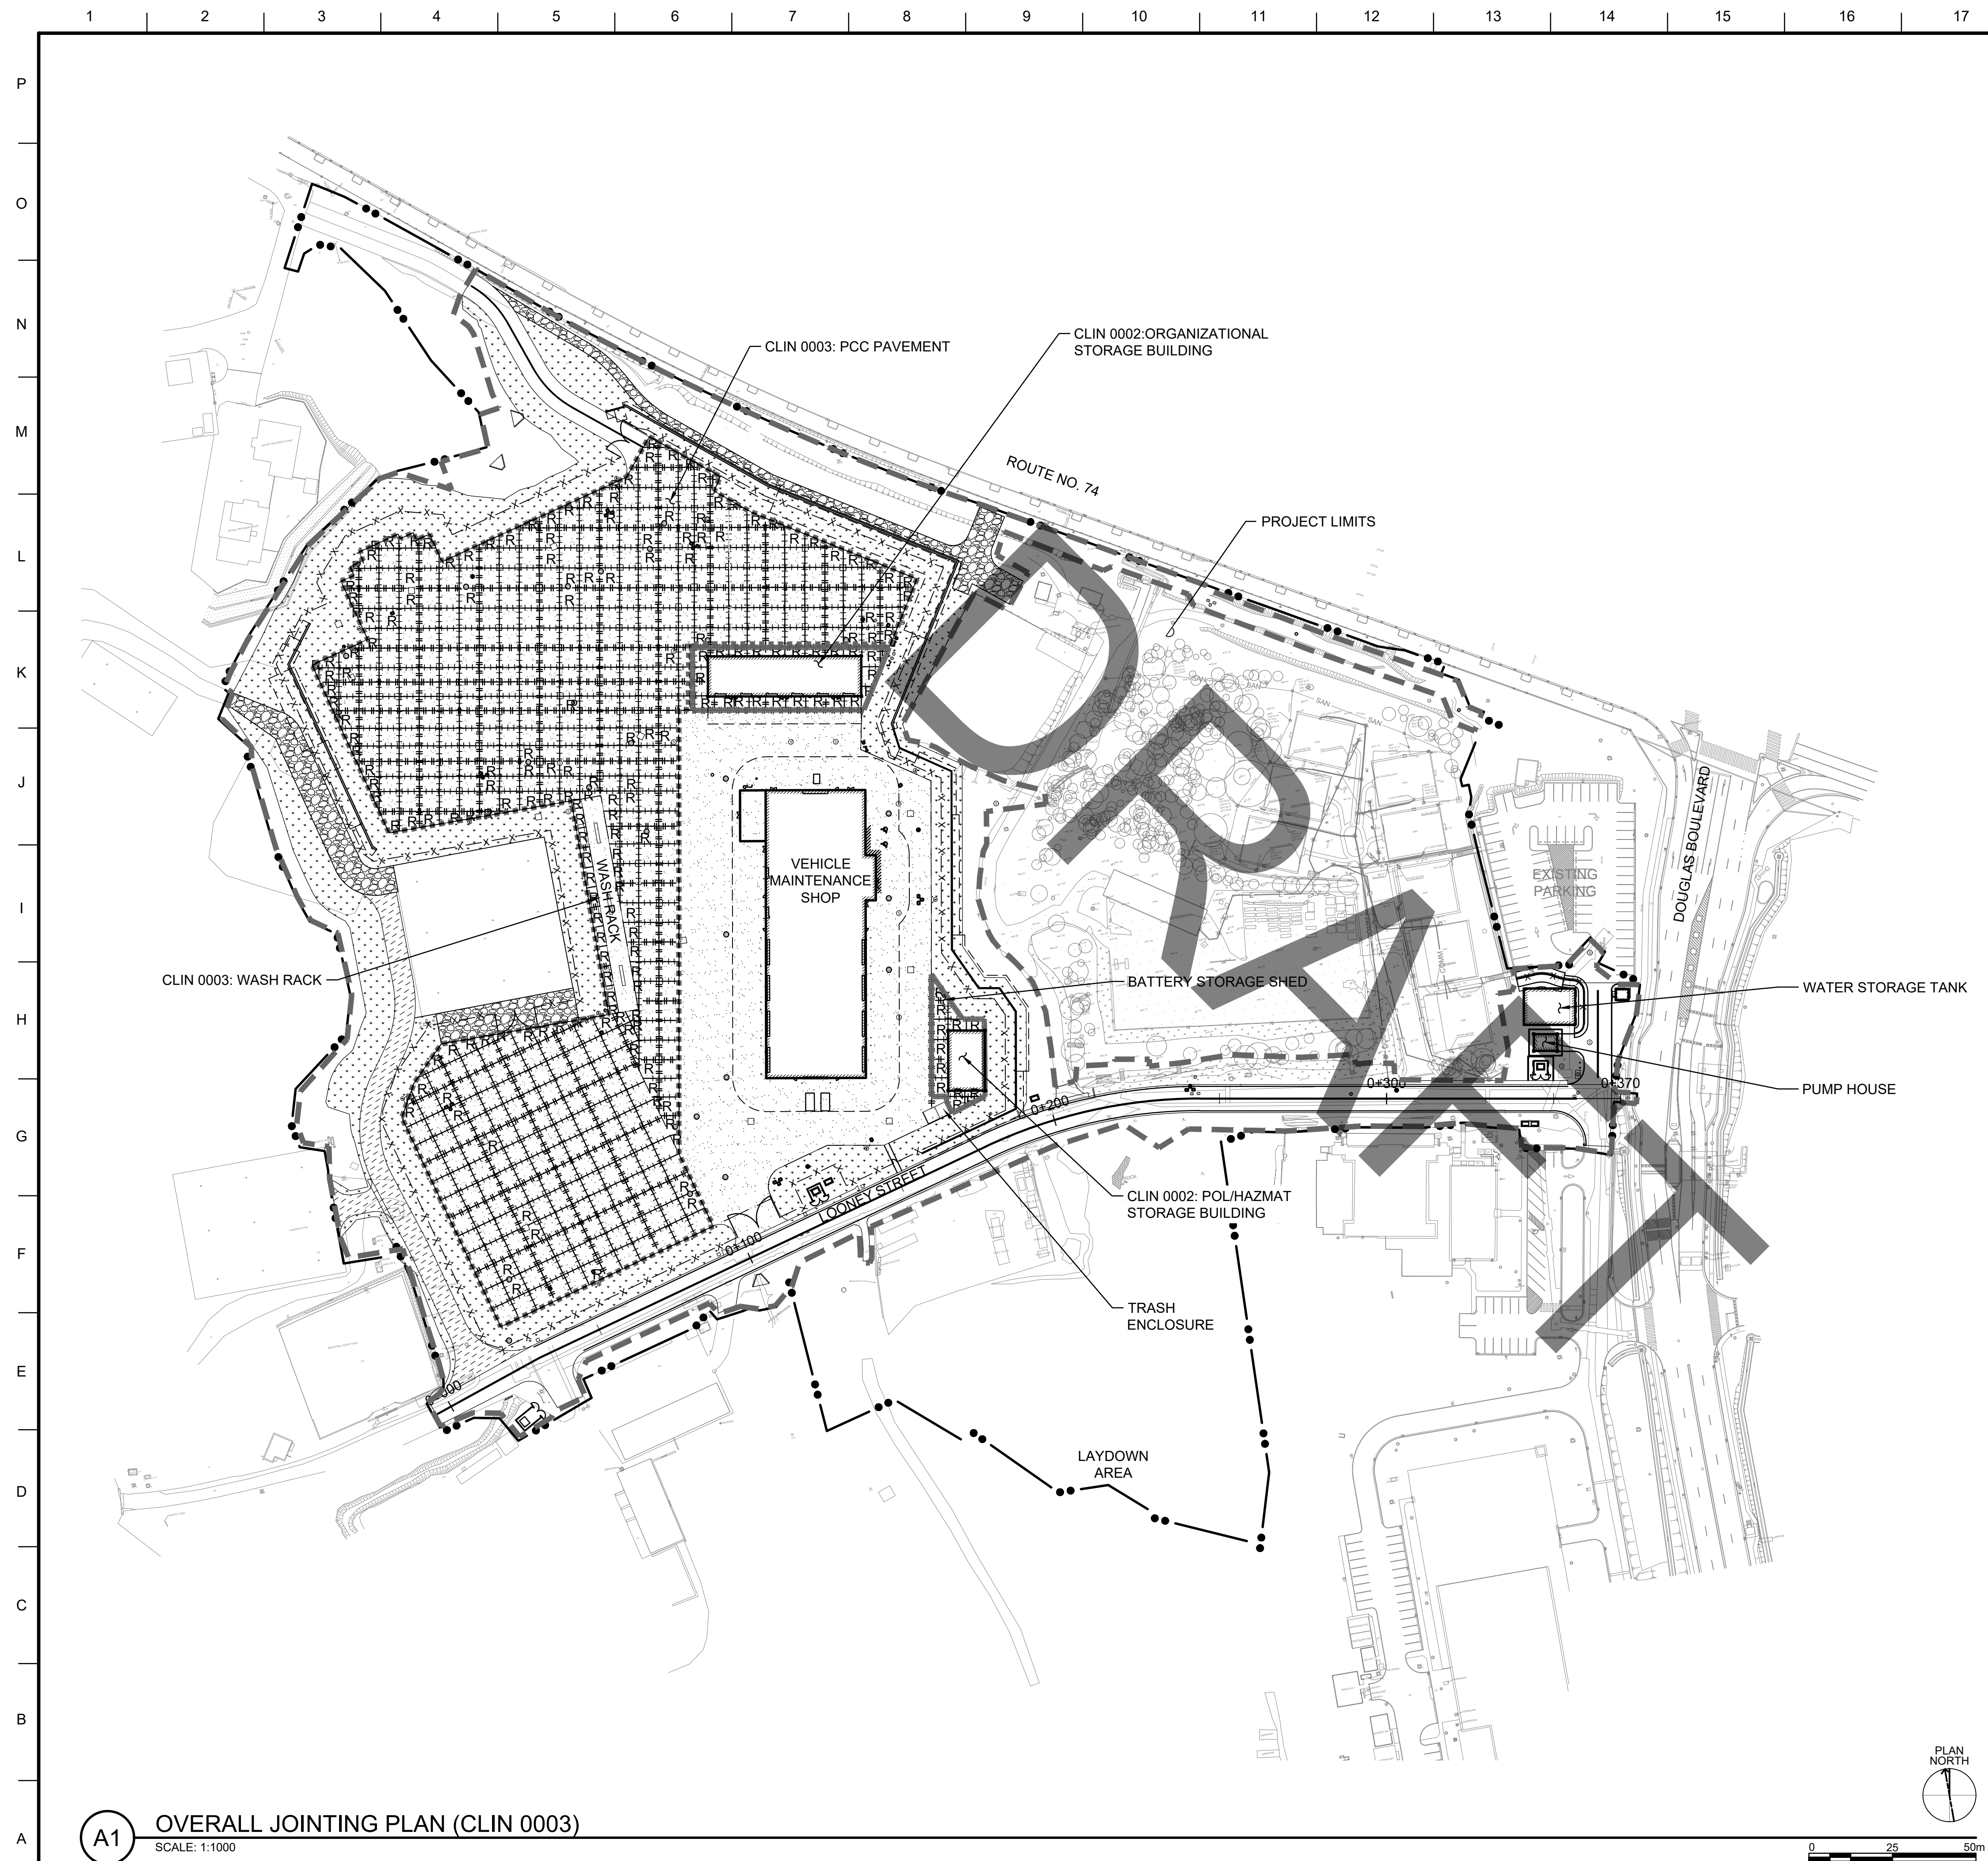

GENERAL NOTES

1. ALL DIMENSIONS SHOWN IN CALLOUT/NOTES ARE IN METERS UNLESS OTHERWISE NOTED.



**U.S. Army Corps
Engineers®**

SHEET LEGEND

- | | |
|---|--|
|  | PROJECT LIMITS |
|  | AC PAVEMENT |
|  | BUILDINGS |
|  | PCC PAVEMENT |
|  | · DOWELED JOINTS |
|  | LONGITUDINAL CONSTRUCTION JOINTS |
|  | TRANSVERSE CONSTRUCTION JOINTS |
|  | SPECIAL REINFORCING, SEE
JOINTING CRITERIA NOTES |
|  | <u>CLIN 0003:</u>
PROVIDE GOV PARKING, WASH RACK AND
PCC PAVEMENT IN LIEU OF ASPHALT
CONCRETE PAVEMENT WITHIN CLIN 0003
LIMITS |

DRAWN BY:	SOLICITATION NO.:	
CHECKED BY:	CONTRACT NO.:	
SUBMITTED BY:	SCALE: AS SHOWN	
SIZE:	FILE NAME:	
ISO A1		

USAED-I, UNIT 35132
APO, AP 96374-5132


SSFM International
SSFM INTERNATIONAL, INC
01 SUMNER STREET, SUITE 620
HONOLULU, HAWAII 96817

FY20 MCA PN77833


OVERALL JOINTING PLAN (CLIN 0003)

SHEET ID
CP154

KEY PLAN

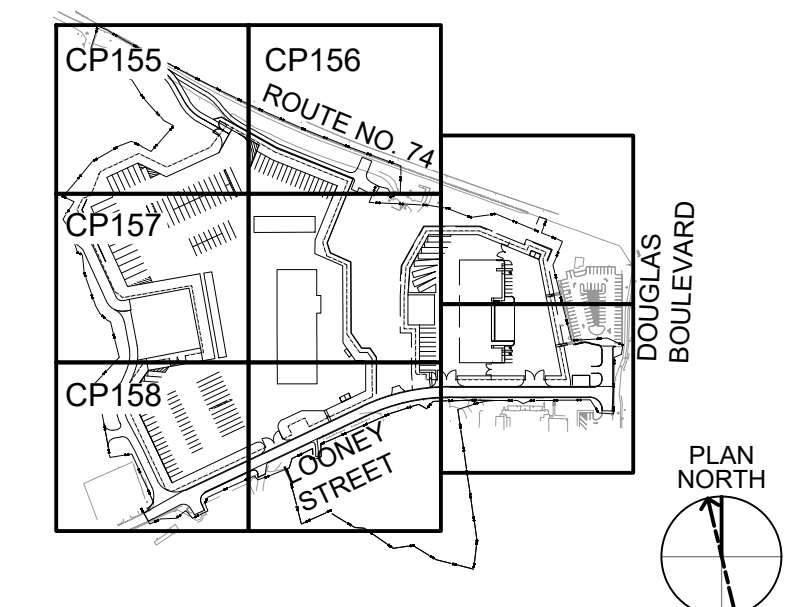

INTERMEDIATE DESIGN

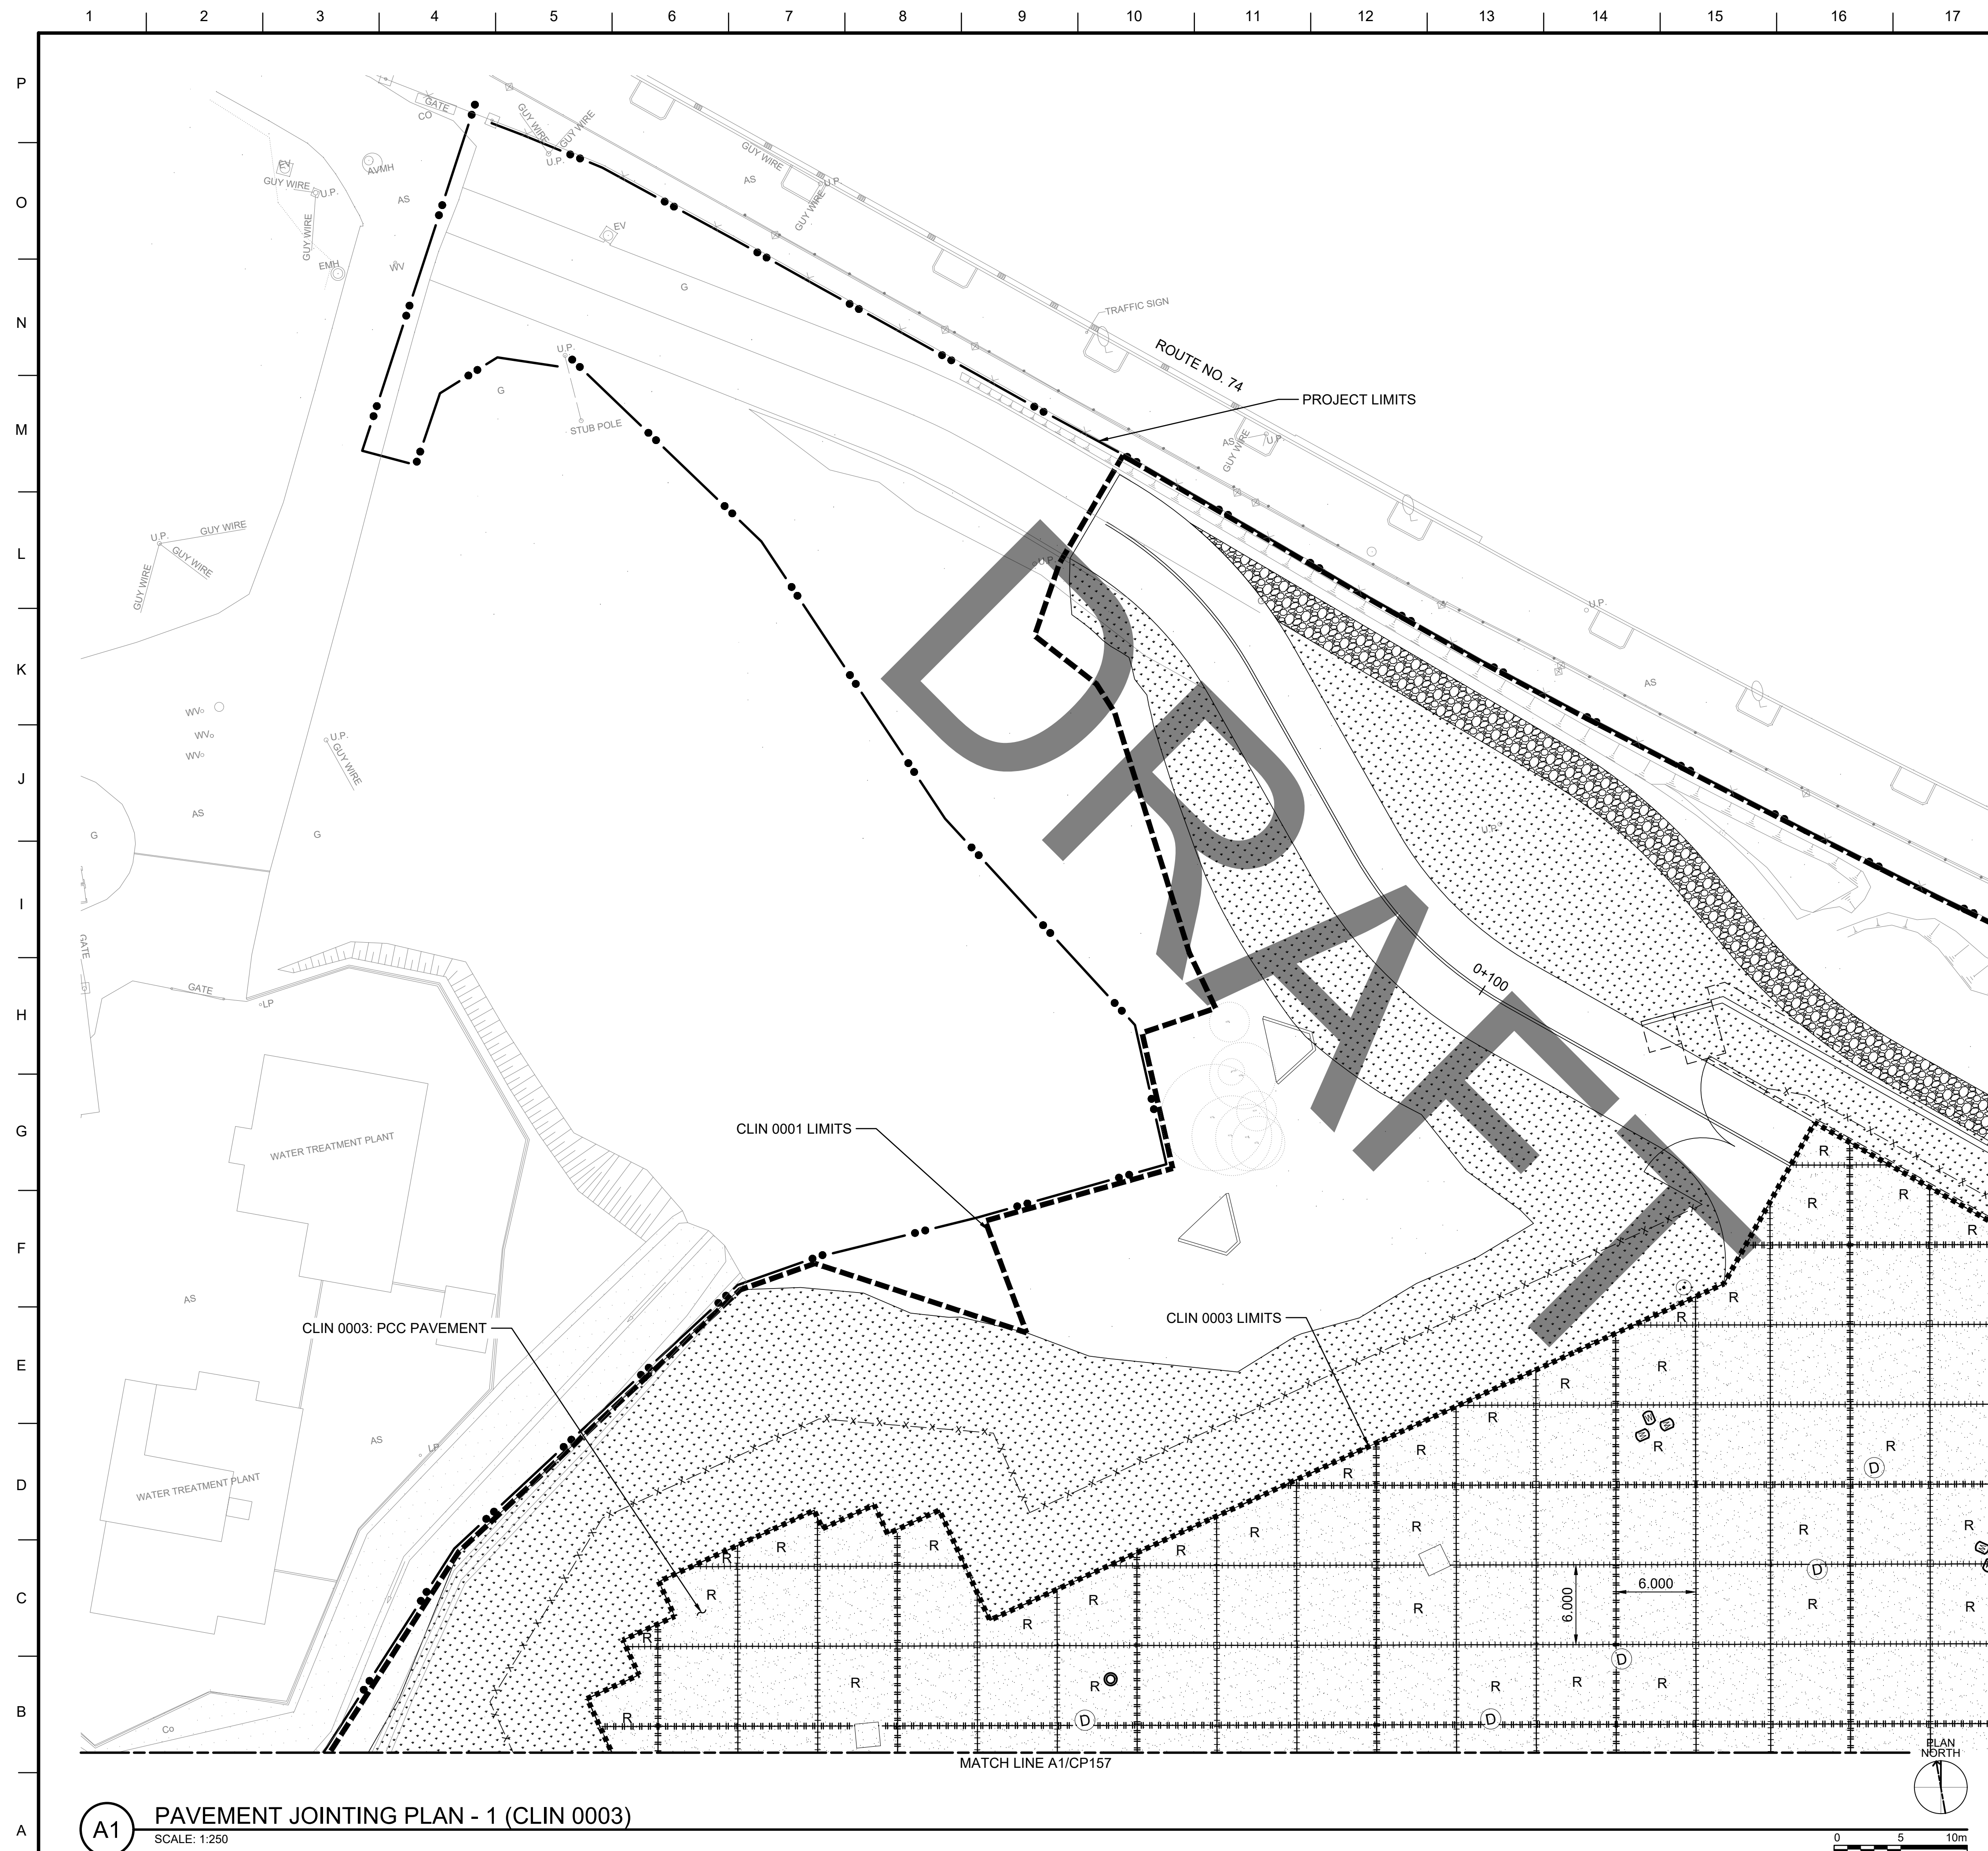

GENERAL NOTES

1. ALL DIMENSIONS SHOWN IN CALLOUT/NOTES ARE IN METERS UNLESS OTHERWISE NOTED.




**U.S. Army Corps
Engineers®**

SHEET LEGEND

- | | |
|---|--|
|  | PROJECT LIMITS |
|  | AC PAVEMENT |
|  | BUILDINGS |
|  | PCC PAVEMENT |
|  | DOWELED JOINTS |
|  | LONGITUDINAL CONSTRUCTION JOINTS |
|  | TRANVERSE CONSTRUCTION JOINTS |
|  | SPECIAL REINFORCING, SEE
JOINTING CRITERIA NOTES |
|  | <u>CLIN 0003:</u>
PROVIDE GOV PARKING, WASH RACK AND
PCC PAVEMENT IN LIEU OF ASPHALT
CONCRETE PAVEMENT WITHIN CLIN 0003
LIMITS |

KEY PLAN

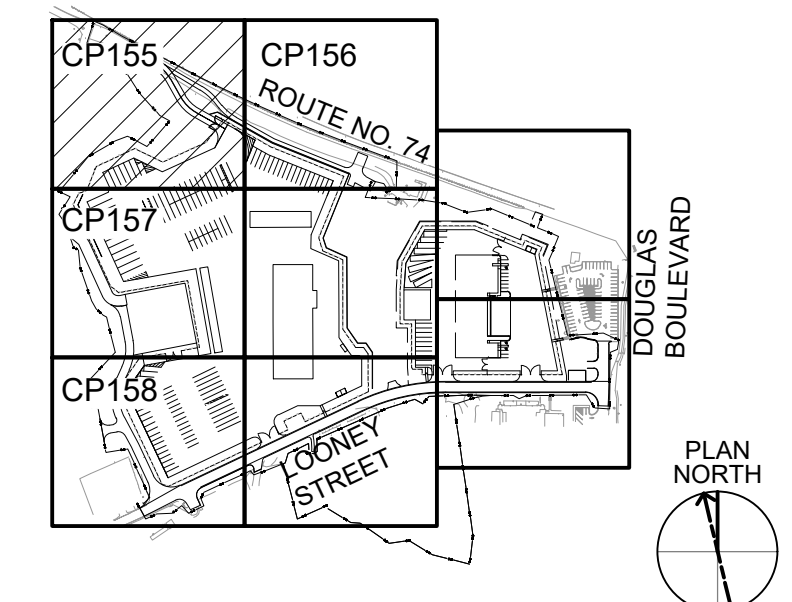


 SSM INTERNATIONAL, INC. 501 SUMNER STREET, SUITE 620 HONOLULU, HAWAII 96817	DRAWN BY:	SOLICITATION NO.:
	CHECKED BY:	CONTRACT NO.:
	SUBMITTED BY:	SCALE:
	SIZE: ISO A1	FILE NAME: AS SHOWN

PAVEMENT JOINTING PLAN - 1 (CLIN 0003)
NADEGAIR BASE, OKINAWA, JAPAN
VEHICLE MAINTENANCE SHOP
FY20 MCA PN77833

SHEET ID
CP155


INTERMEDIATE DESIGN

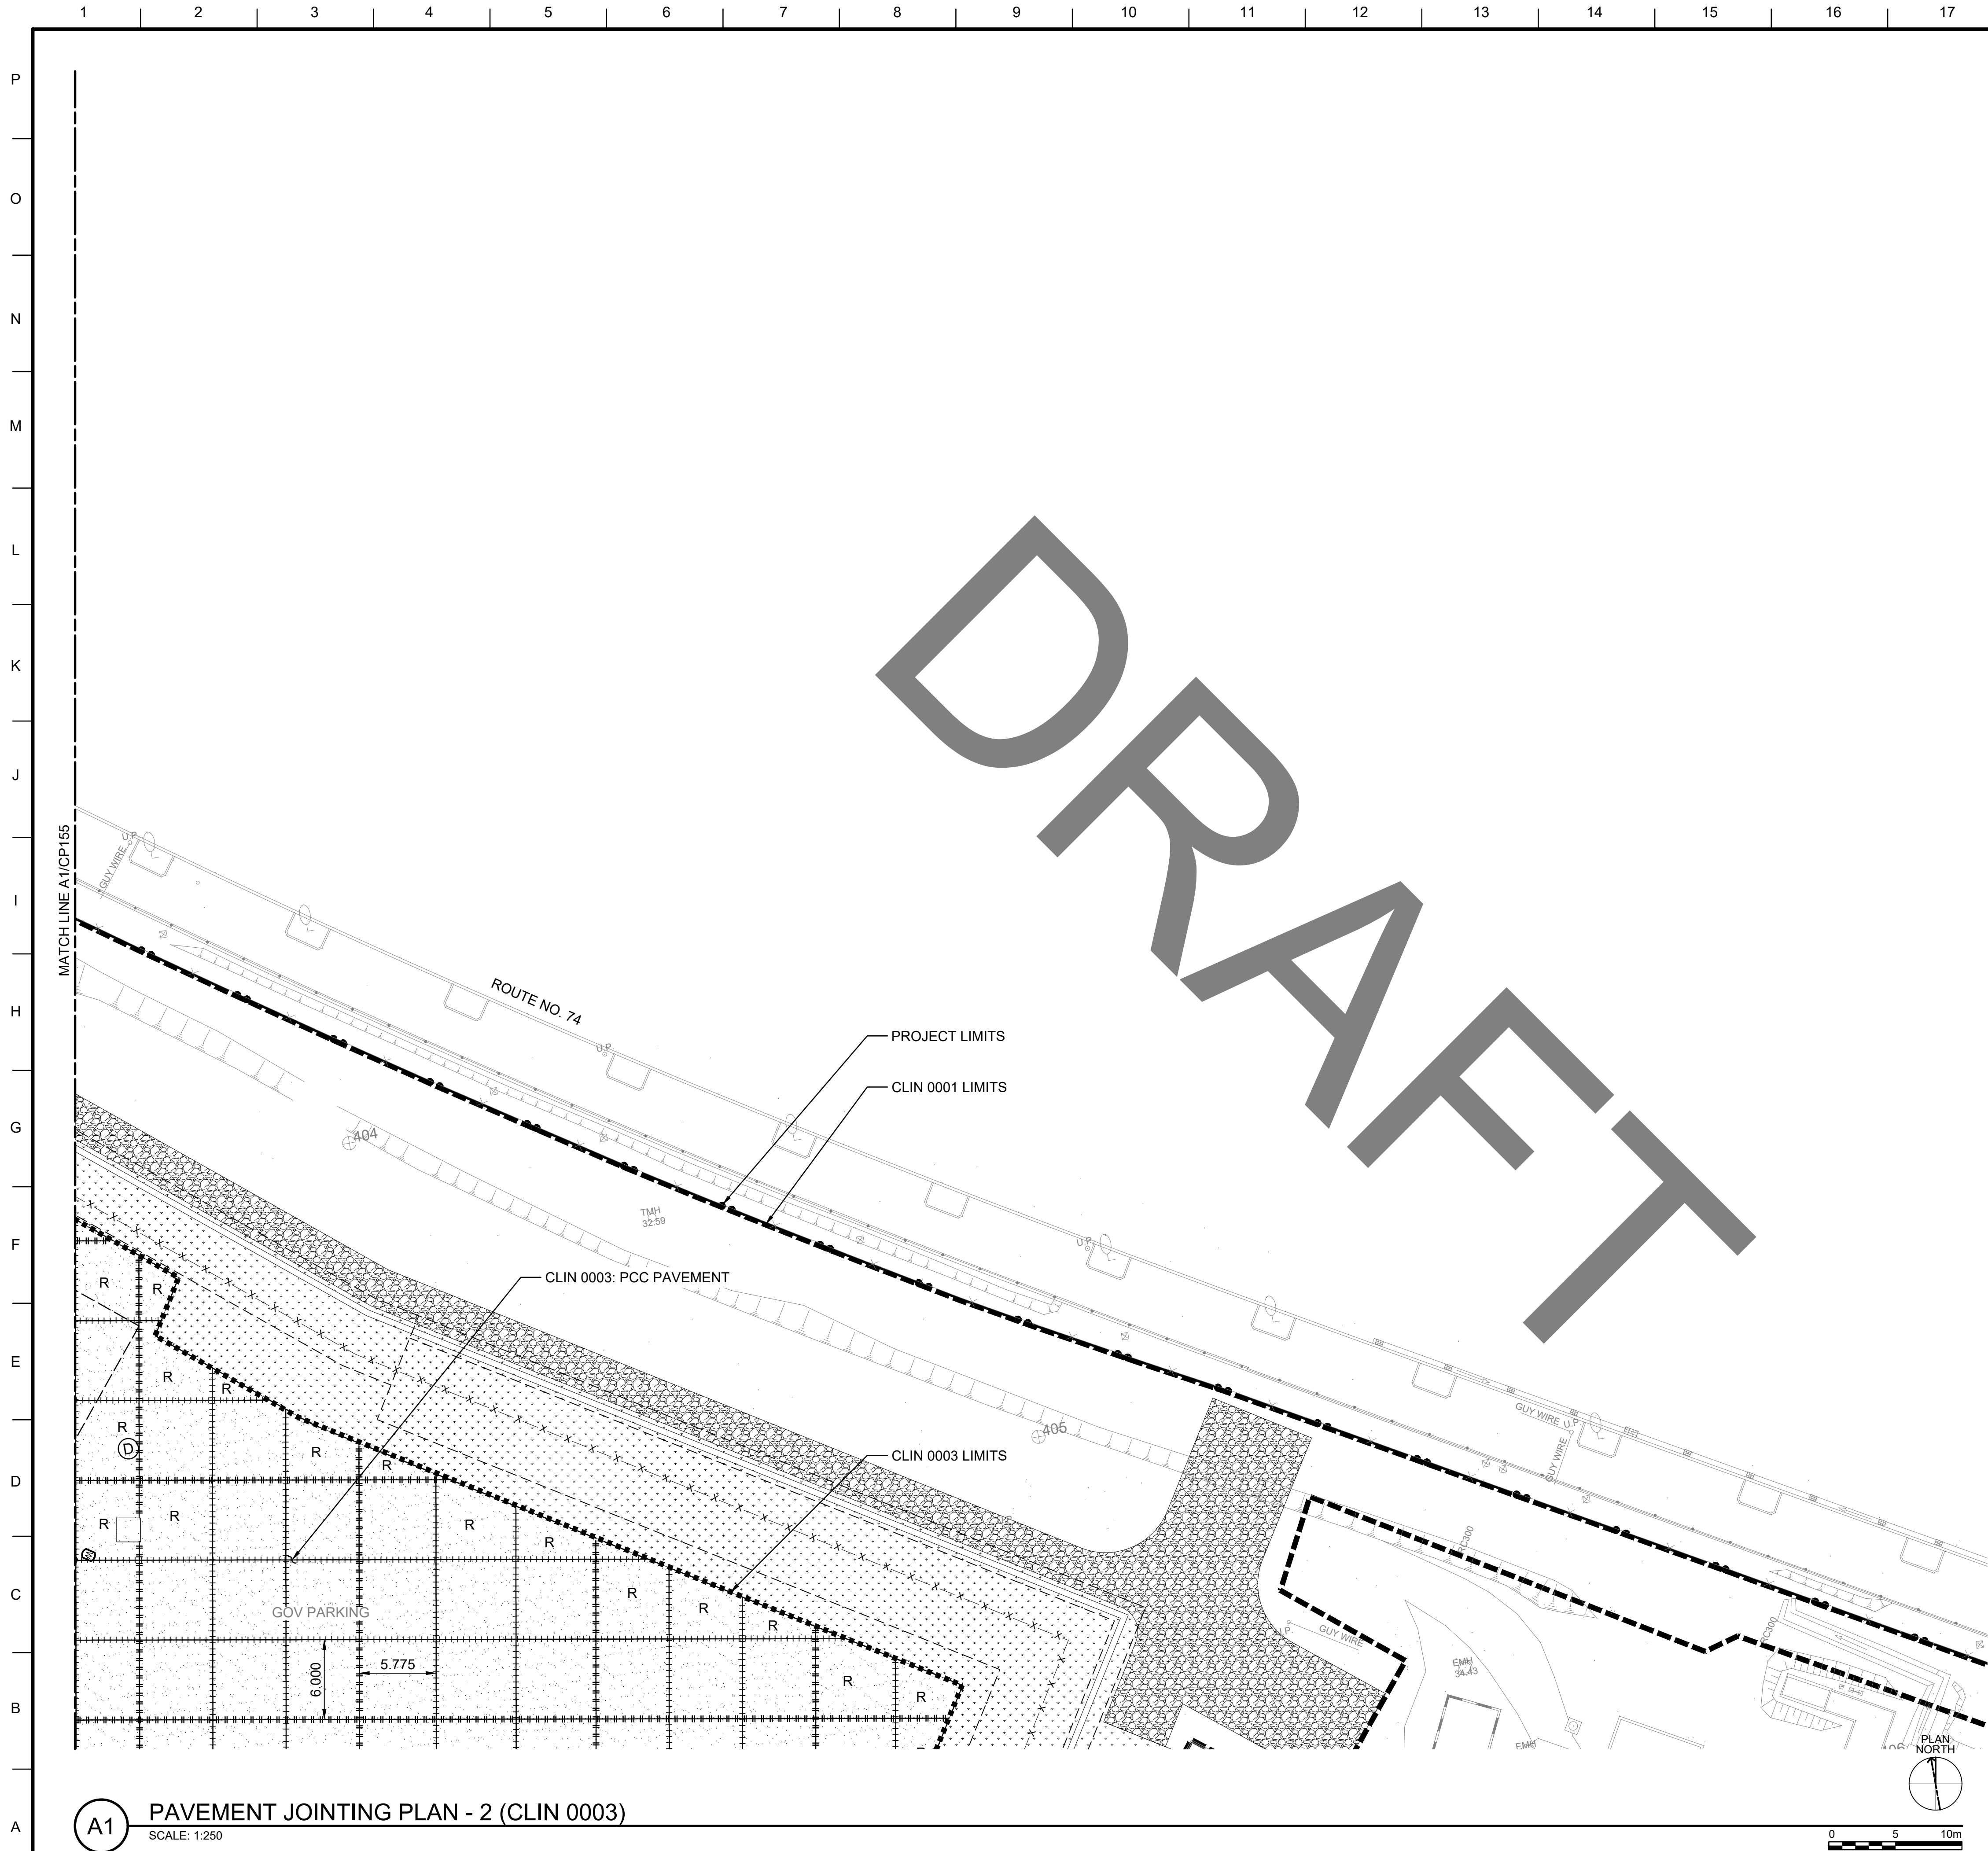

A1 PAVEMENT JOINTING PLAN - 2 (CLIN 0003)
SCALE: 1:250

GENERAL NOTES

1. ALL DIMENSIONS SHOWN IN CALLOUT/NOTES ARE IN METERS UNLESS OTHERWISE NOTED.

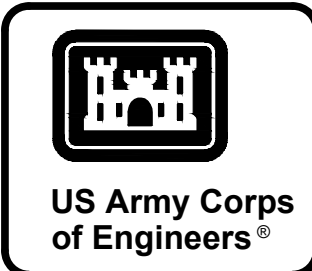


SHEET LEGEND

- PROJECT LIMITS
- AC PAVEMENT
- BUILDINGS
- PCC PAVEMENT
- DOWELED JOINTS
- LONGITUDINAL CONSTRUCTION JOINTS
- TRANVERSE CONSTRUCTION JOINTS
- SPECIAL REINFORCING, SEE JOINTING CRITERIA NOTES
- CLIN 0003: PROVIDE GOV PARKING, WASH RACK AND PCC PAVEMENT IN LIEU OF ASPHALT CONCRETE PAVEMENT WITHIN CLIN 0003 LIMITS

CLIN 0003

KEY PLAN

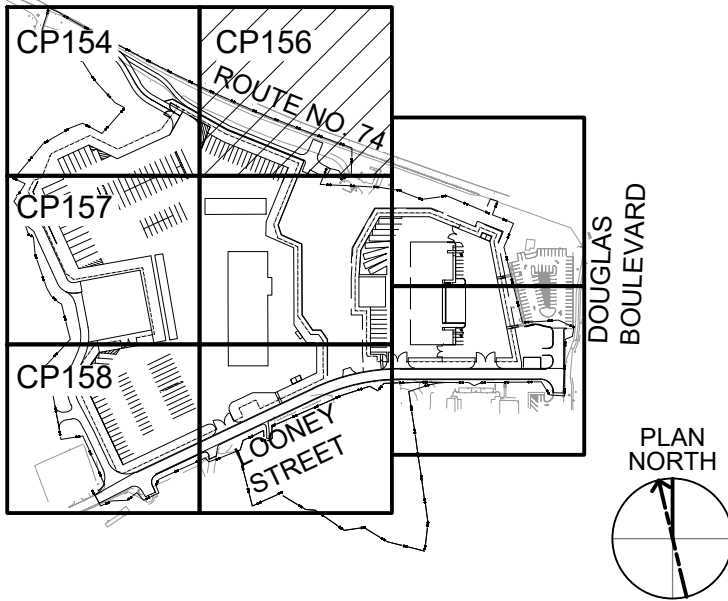


DESIGNED BY:	ISSUE DATE:
DRAWN BY:	SOLICITATION NO.:
CHECKED BY:	CONTRACT NO.:
SUBMITTED BY:	SCALE:
SIZE:	FILE NAME:
ISO A1	AS SHOWN

US ARMY CORPS OF ENGINEERS
JAPAN DISTRICT, OKINAWA AREA OFFICE
USAED-J UNIT 35132
APO, AP 96374-5132
SSFM
SSFM INTERNATIONAL, INC.
501 SUMNER STREET, SUITE 620
HONOLULU, HAWAII 96817

KADENA AIR BASE, OKINAWA, JAPAN
VEHICLE MAINTENANCE SHOP
FY20 MCA PN77833
PAVEMENT JOINTING PLAN - 2 (CLIN 0003)

SHEET ID
CP156

INTERMEDIATE DESIGN

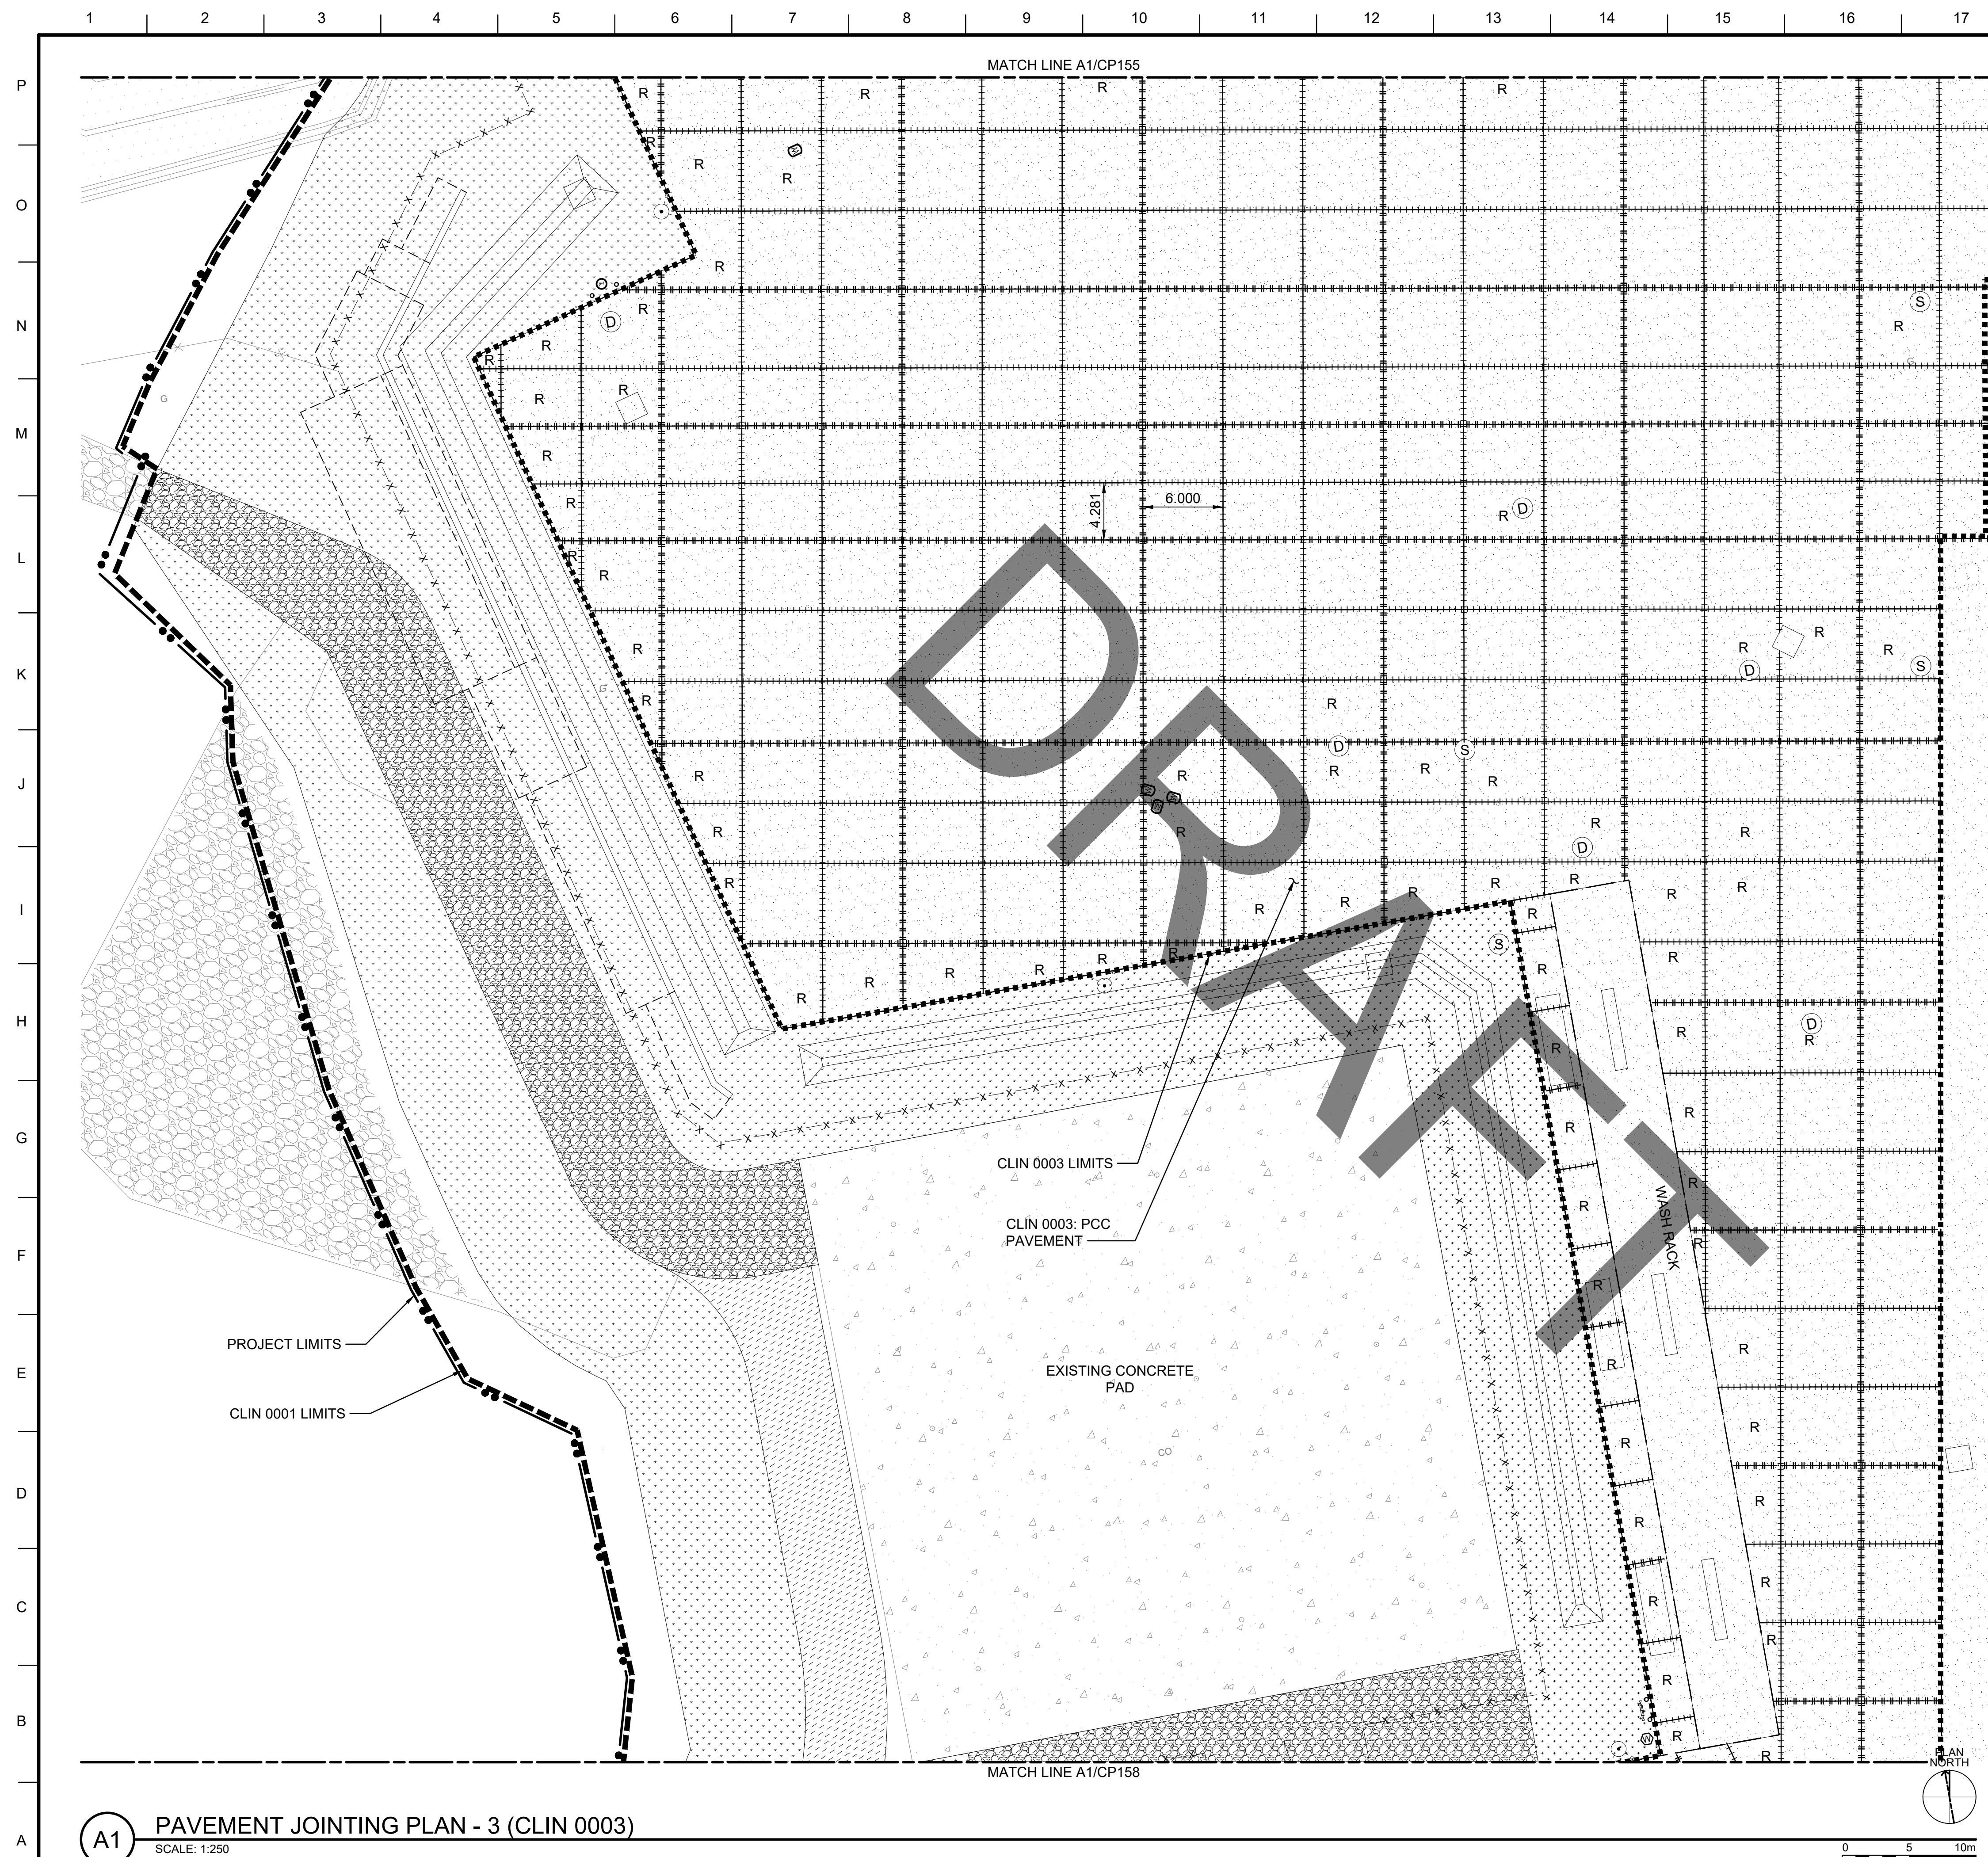



GENERAL NOTES

1. ALL DIMENSIONS SHOWN IN CALLOUT/NOTES ARE IN METERS UNLESS OTHERWISE NOTED.



**S Army Corps
Engineers®**

SHEET LEGEND

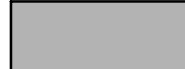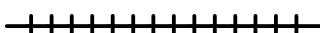- | | |
|---|--|
|  | AC PAVEMENT |
|  | BUILDINGS |
|  | PCC PAVEMENT |
|  | · DOWELED JOINTS |
|  | LONGITUDINAL CONSTRUCTION JOINTS |
|  | TRANSVERSE CONSTRUCTION JOINTS |
|  | SPECIAL REINFORCING, SEE
JOINTING CRITERIA NOTES |
|  | <u>CLIN 0003:</u>
PROVIDE GOV PARKING, WASH RACK AND
PCC PAVEMENT IN LIEU OF ASPHALT
CONCRETE PAVEMENT WITHIN CLIN 0003
LIMITS |

DRAWN BY:	SOLICITATION
-----------	--------------

DRAWN BY: _____

CHECKED BY:	CONTRACT NO.:
-------------	---------------

SUBMITTED BY:	SCALE:
---------------	--------

MARK	DESCRIPTION
------	-------------

OKINAWA AREA OFFICE

USAED-J, UNIT 35132

APO, AP 96374-5132

三上 三上


HONOLULU, HAWAII 96817

MADEIRA AIR BASE, OKINAWA, JAPAN
VEHICLE MAINTENANCE SHOP
FY20 MCA PN77833

PAVEMENT JOINTING PLAN - 3 (CLIN 0003)






SHEET ID

CP157

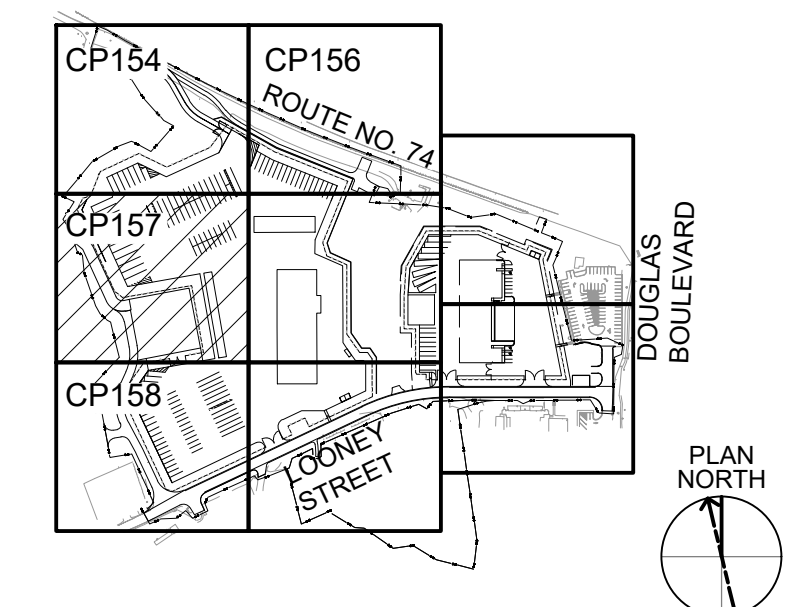

INTERMEDIATE DESIGN





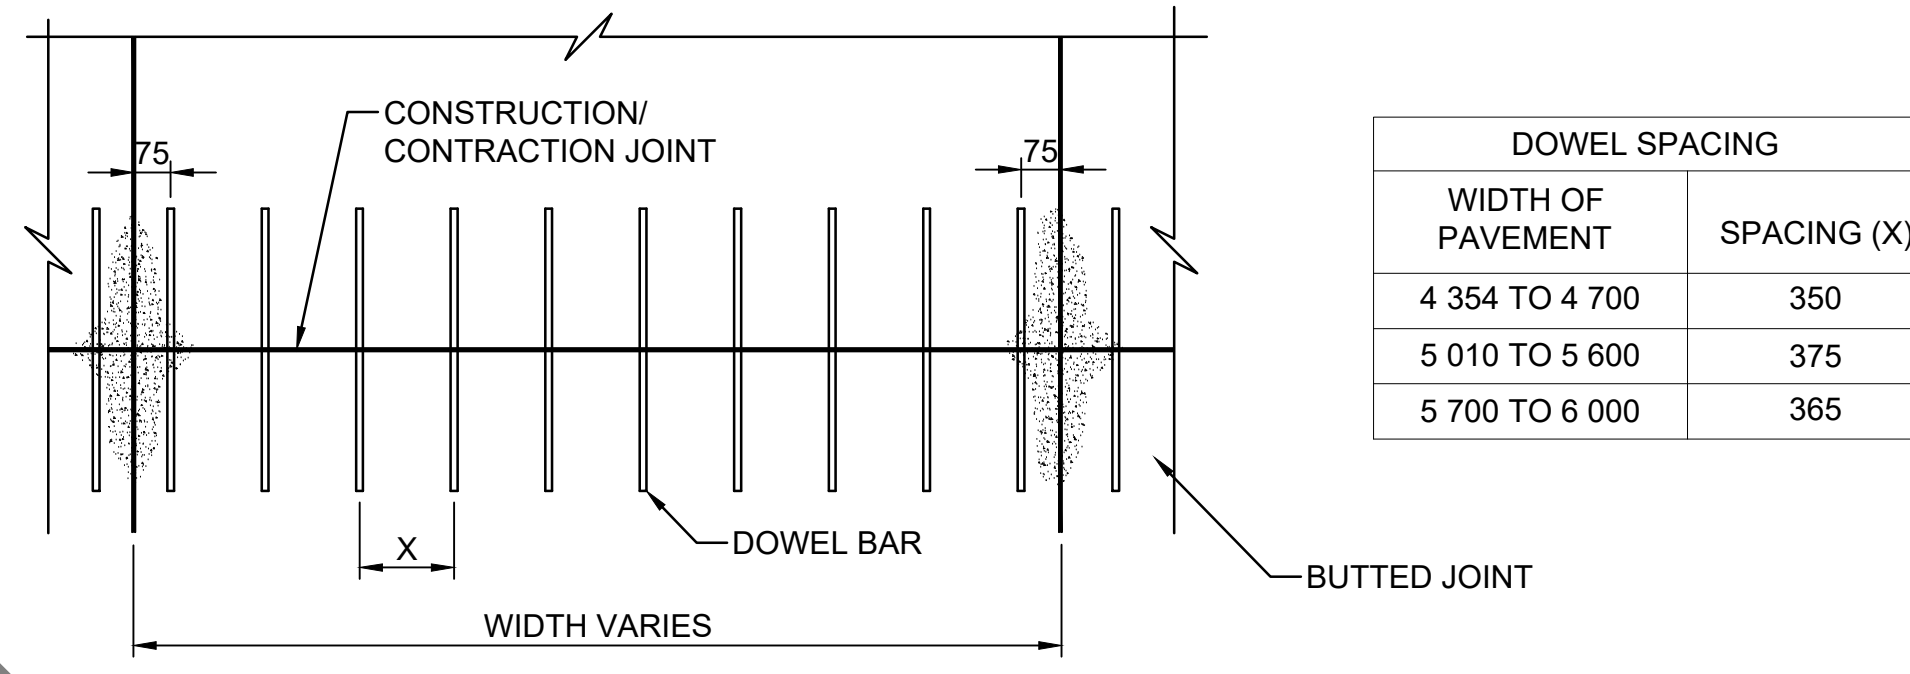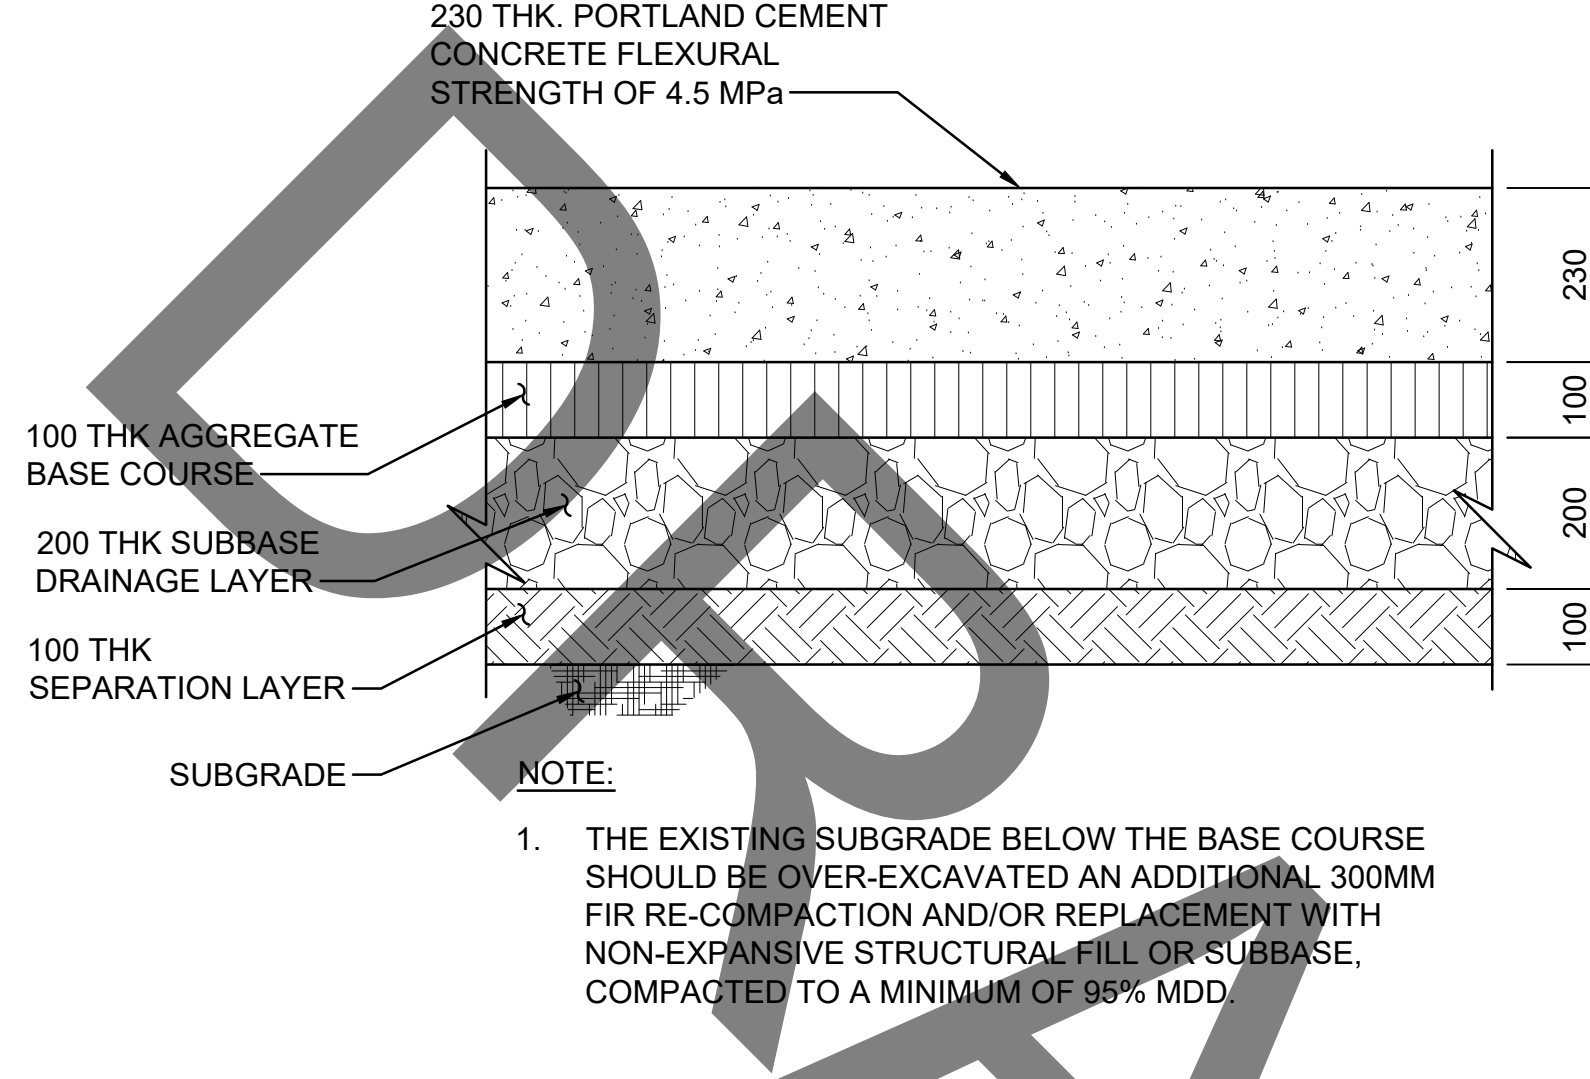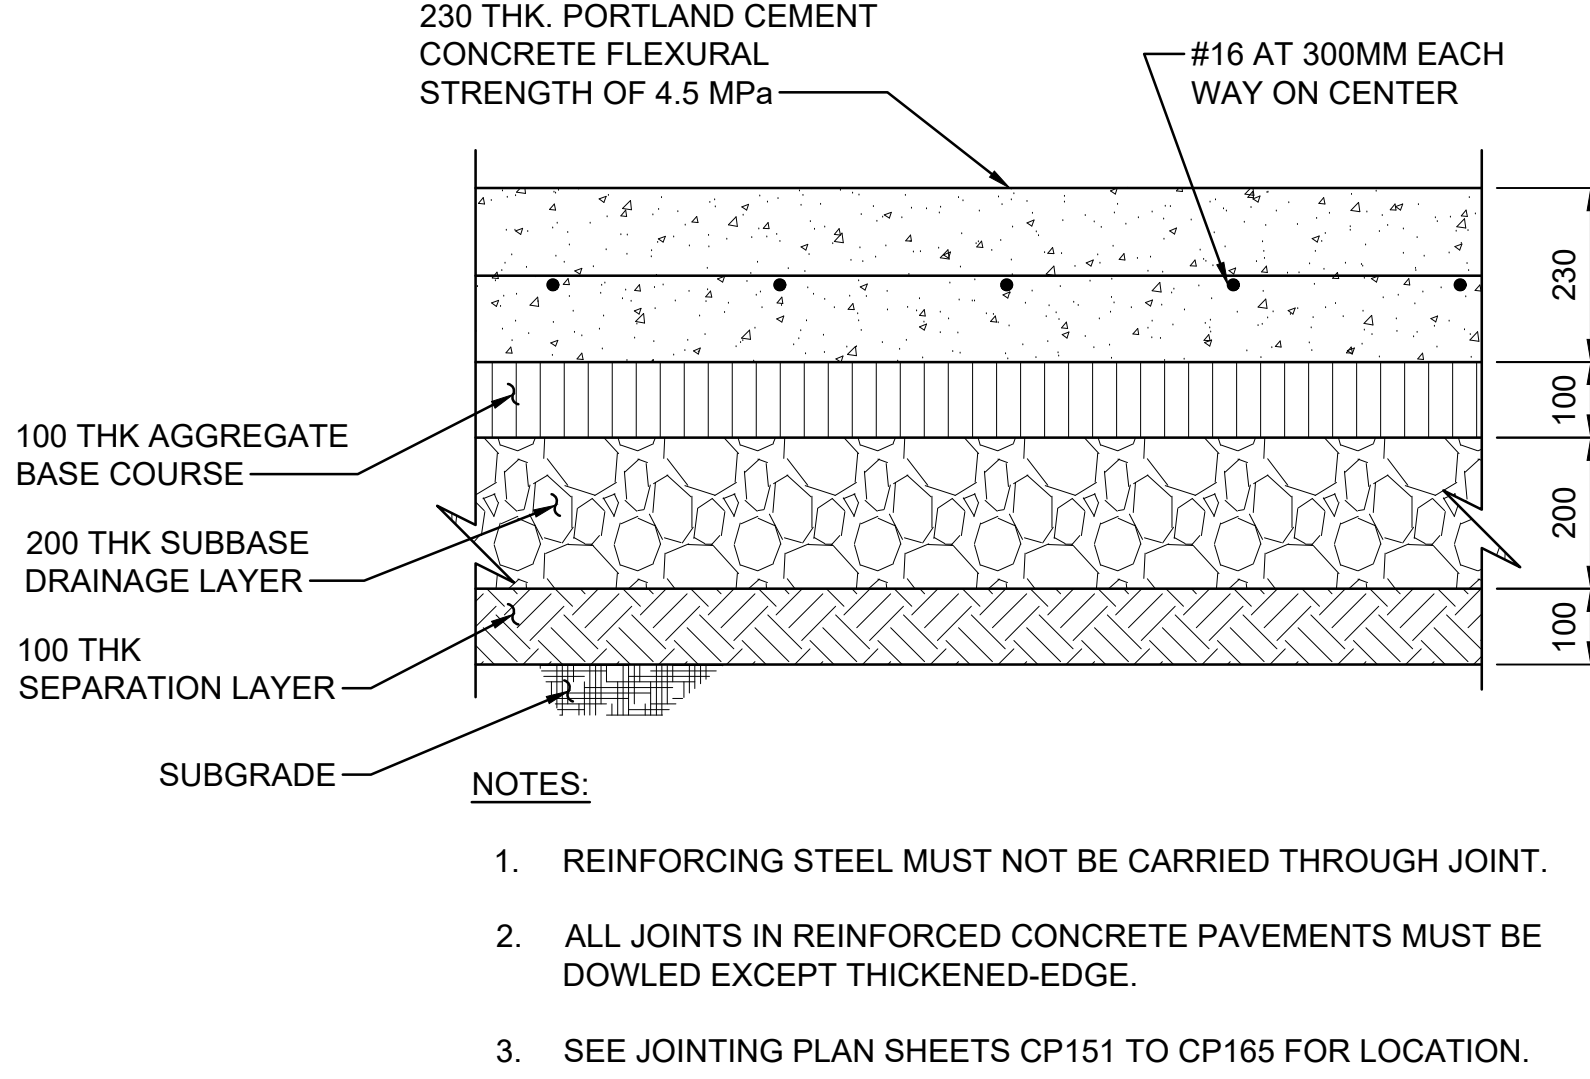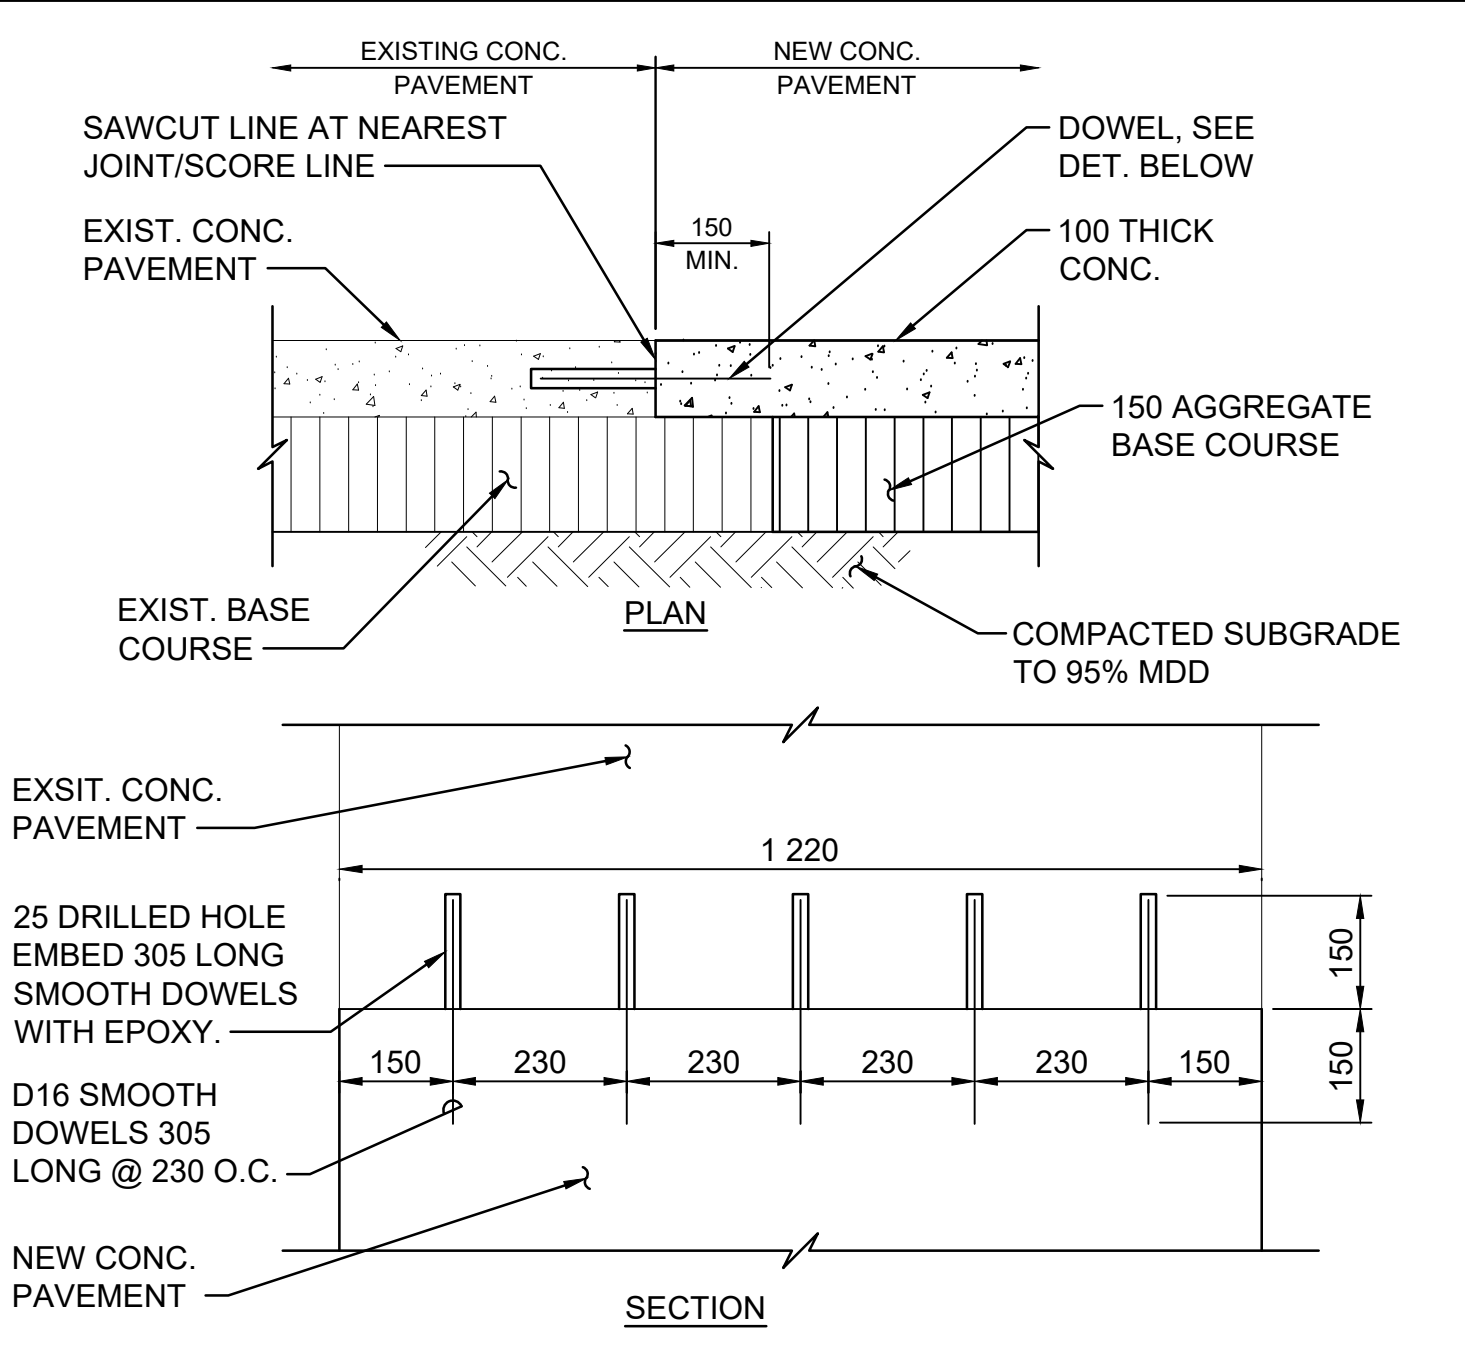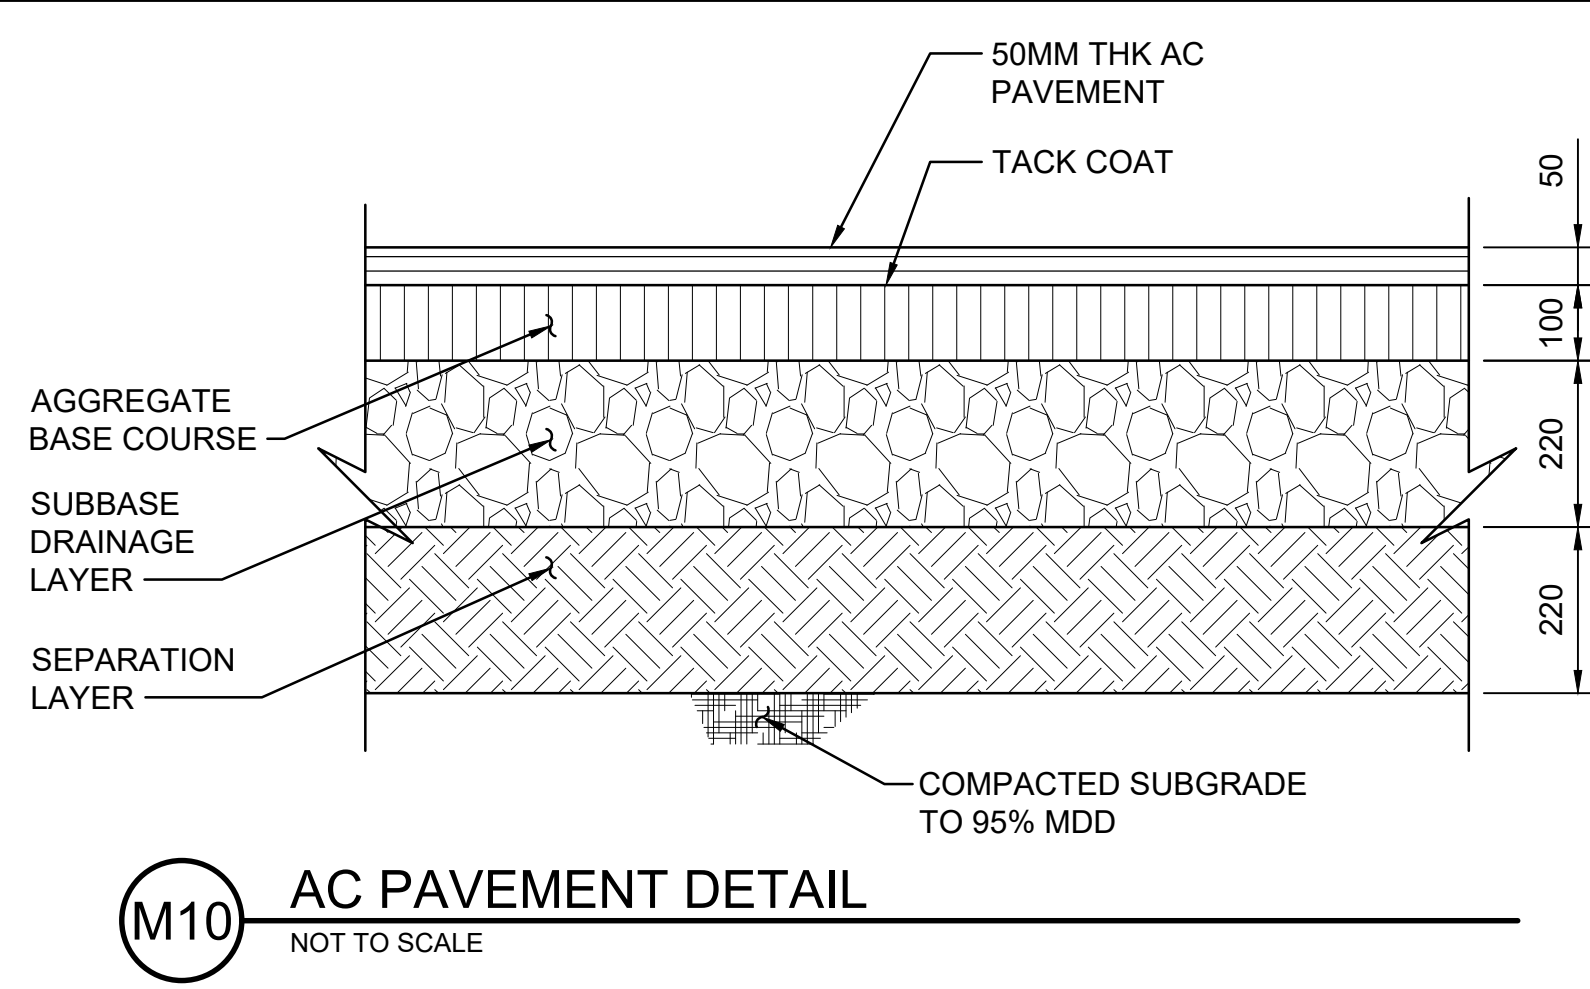

DOWEL SPACING	
WIDTH OF PAVEMENT	SPACING (X)
4 354 TO 4 700	350
5 010 TO 5 600	375
5 700 TO 6 000	365


- NOTES:
1. REINFORCING STEEL MUST NOT BE CARRIED THROUGH JOINT.
 2. ALL JOINTS IN REINFORCED CONCRETE PAVEMENTS MUST BE DOWLED EXCEPT THICKENED-EDGE.
 3. SEE JOINTING PLAN SHEETS CP151 TO CP165 FOR LOCATION.

- NOTE:
1. THE EXISTING SUBGRADE BELOW THE BASE COURSE SHOULD BE OVER-EXCAVATED AN ADDITIONAL 300MM FOR RE-COMPACT AND/OR REPLACEMENT WITH NON-EXPANSIVE STRUCTURAL FILL OR SUBBASE, COMPACTED TO A MINIMUM OF 98% MDD.

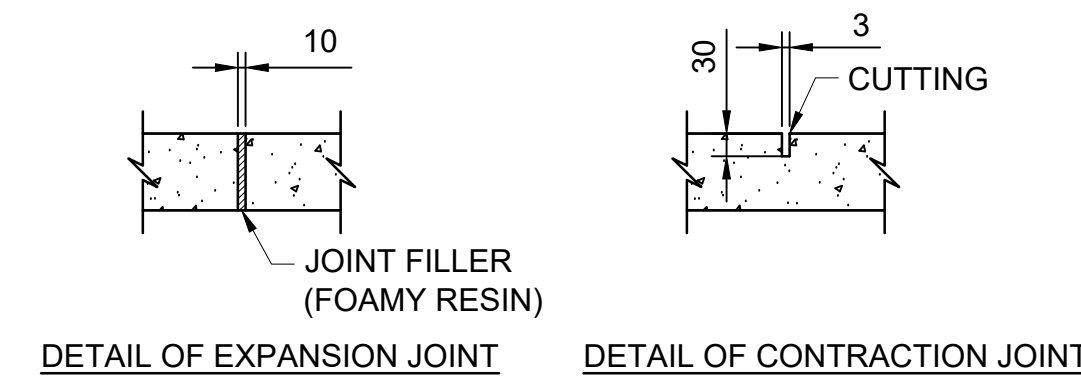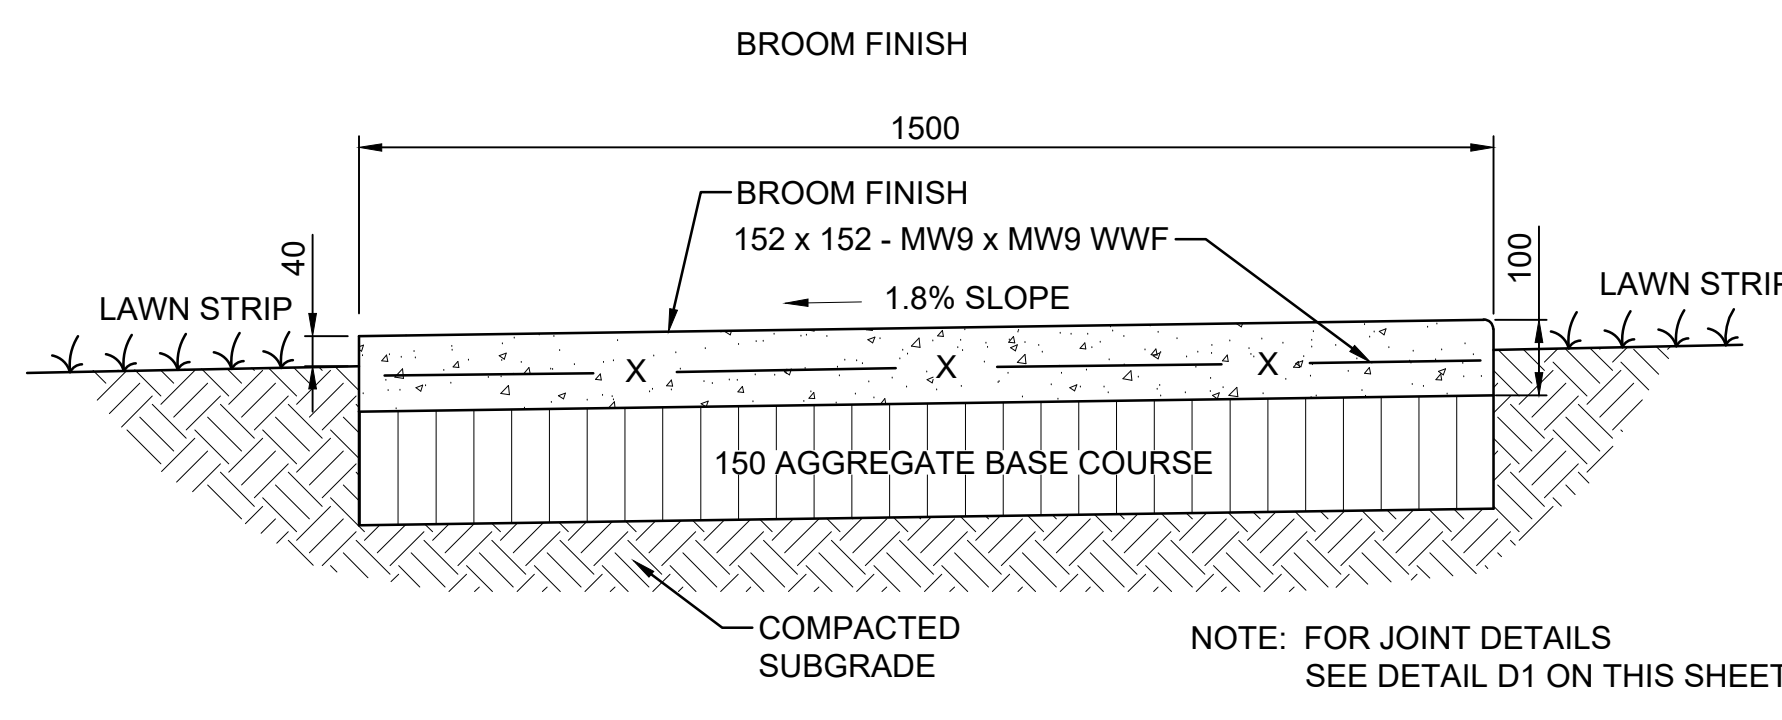

JOINT INSTALLATION SITE	
JOINT TYPE	INSTALLATION SITE
CONTRACTION	AT EVERY 1.5 METERS
EXPANSION	AT EVERY 6 CONTRACTION JOINT SPANS AT INTERSECTION OF SIDEWALK AT IRREGULAR SHAPE SECTION

NOTE: SIDEWALK SURFACE MUST BE BROOM FINISHED.

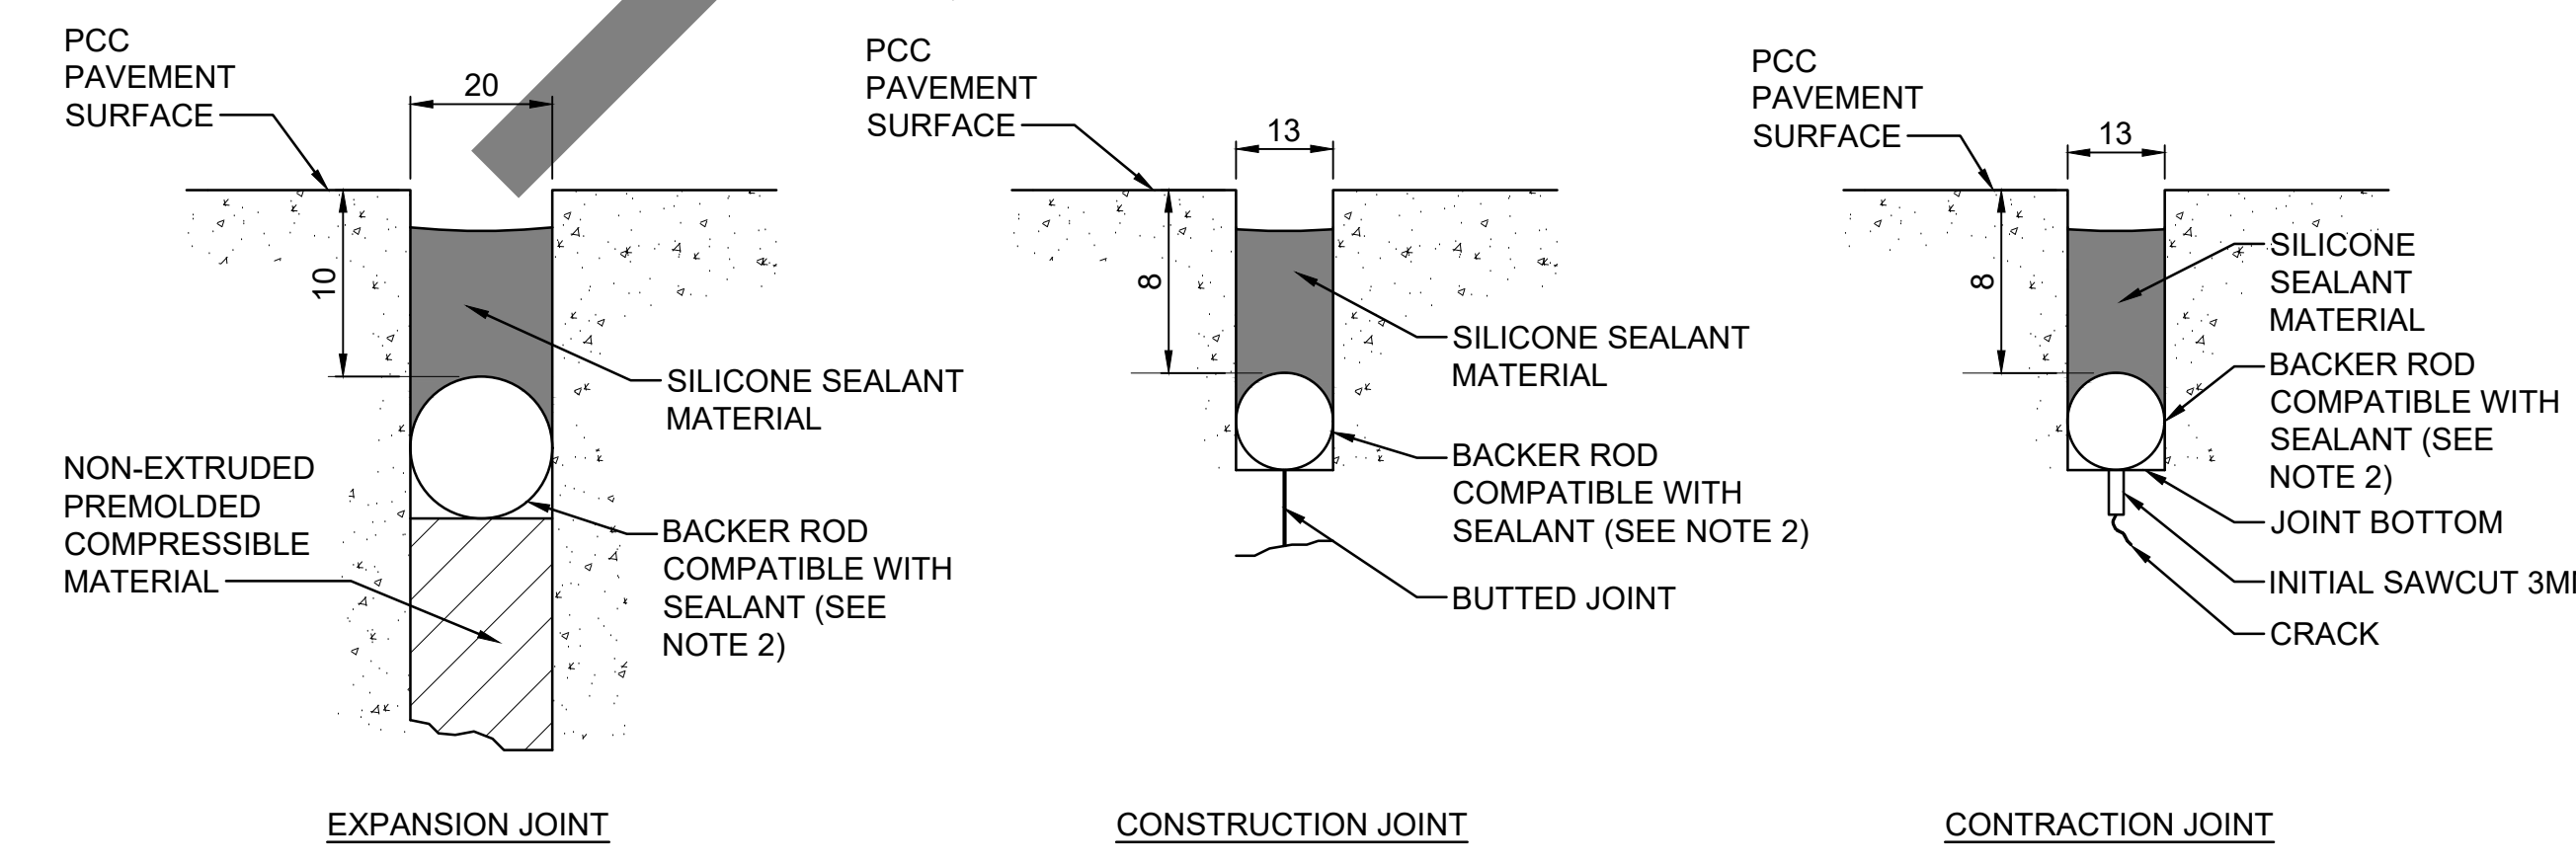

- NOTES:
1. TOP OF SEALANT SHALL BE 2MM TO 6MM BELOW TOP OF PAVEMENT. IN AREAS TO BE GROOVED, THE JOINT SEAL SHALL BE RECESSED BELOW THE DEPTH OF THE GROOVES.
 2. BACKER ROD MATERIAL MUST BE COMPATIBLE WITH THE TYPE OF SEALANT USED AND SIZED TO PROVIDE THE DESIRED SHAPE FACTOR.

US Army Corps of Engineers®

ISSUE DATE:	DESIGNED BY:	US ARMY CORPS OF ENGINEERS
SOLICITATION NO.:	DRAWN BY:	JAPAN DISTRICT, OKINAWA AREA OFFICE
CONTRACT NO.:	CHECKED BY:	USAED-J UNIT 35132
SCALE:	SUBMITTED BY:	APO, AP 96374-5132
AS SHOWN	FILE NAME:	SSFM INTERNATIONAL, INC.
	SIZE:	501 SUMNER STREET, SUITE 620
	ISO A1	HONOLULU, HAWAII 96817


KADENA AIR BASE, OKINAWA, JAPAN

VEHICLE MAINTENANCE SHOP


FY20 MCA PN77833

PAVEMENT DETAILS - 1

SHEET ID
TEMP
CP501

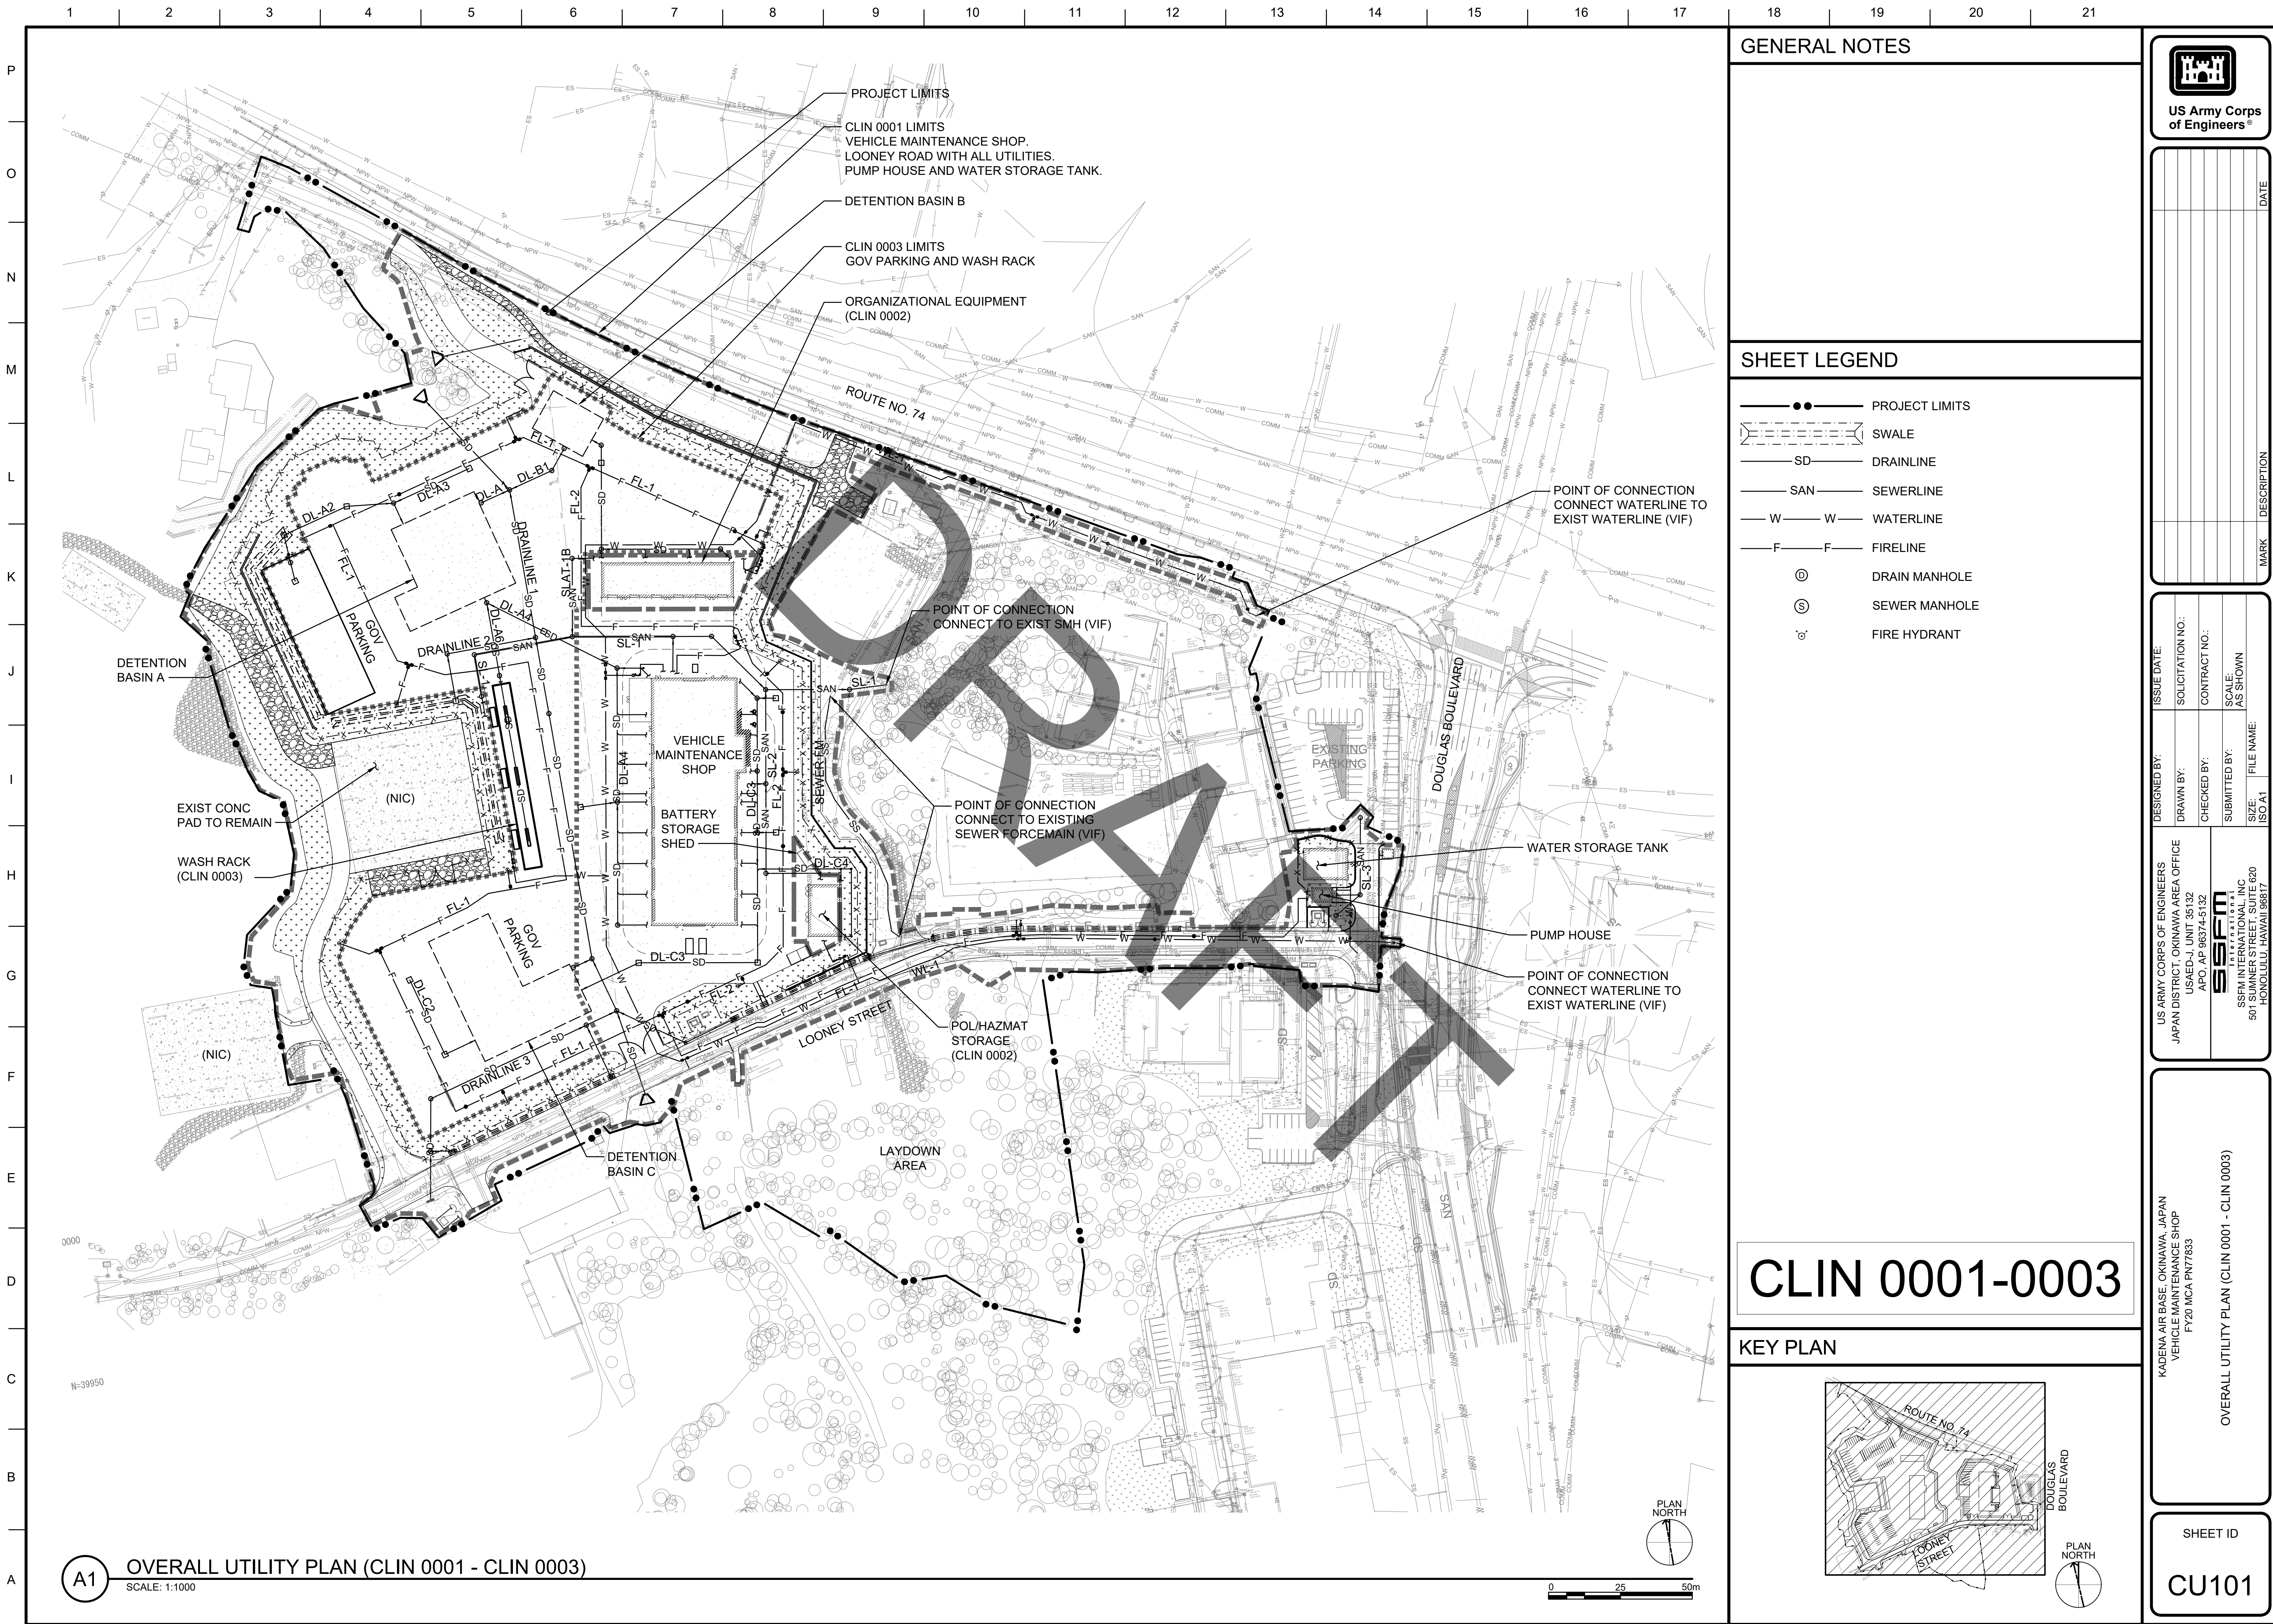

GENERAL NOTES

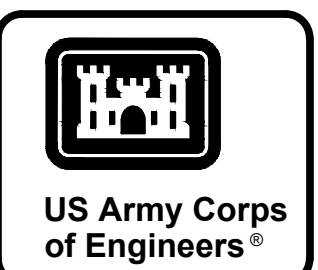


US Army Corps
of Engineers®

SHEET LEGEND

- PROJECT LIMITS
- SWALE
- DRAINLINE
- SAN SEWERLINE
- W WATERLINE
- F FIRELINE
- DRAIN MANHOLE
- SEWER MANHOLE
- FIRE HYDRANT

CLIN 0001-0003

KEY PLAN

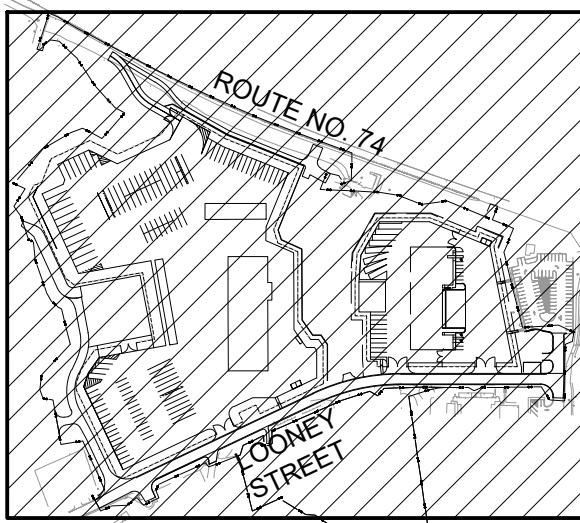

DESIGNED BY:	ISSUE DATE:
DRAWN BY:	SOLICITATION NO.:
CHECKED BY:	CONTRACT NO.:
SUBMITTED BY:	SCALE:
FILE NAME:	AS SHOWN
SIZE:	ISO A1


US ARMY CORPS OF ENGINEERS
JAPAN DISTRICT, OKINAWA AREA OFFICE
USAED-J, UNIT 35132
APO, AP 96374-5132

SSM
SSM INTERNATIONAL, INC.
501 SUMNER STREET, SUITE 620
HONOLULU, HAWAII 96817

KADENA AIR BASE, OKINAWA, JAPAN VEHICLE MAINTENANCE SHOP FY20 MCA PN77833	OVERALL UTILITY PLAN (CLIN 0001 - CLIN 0003)
---	--


SHEET ID
CU101

INTERMEDIATE DESIGN

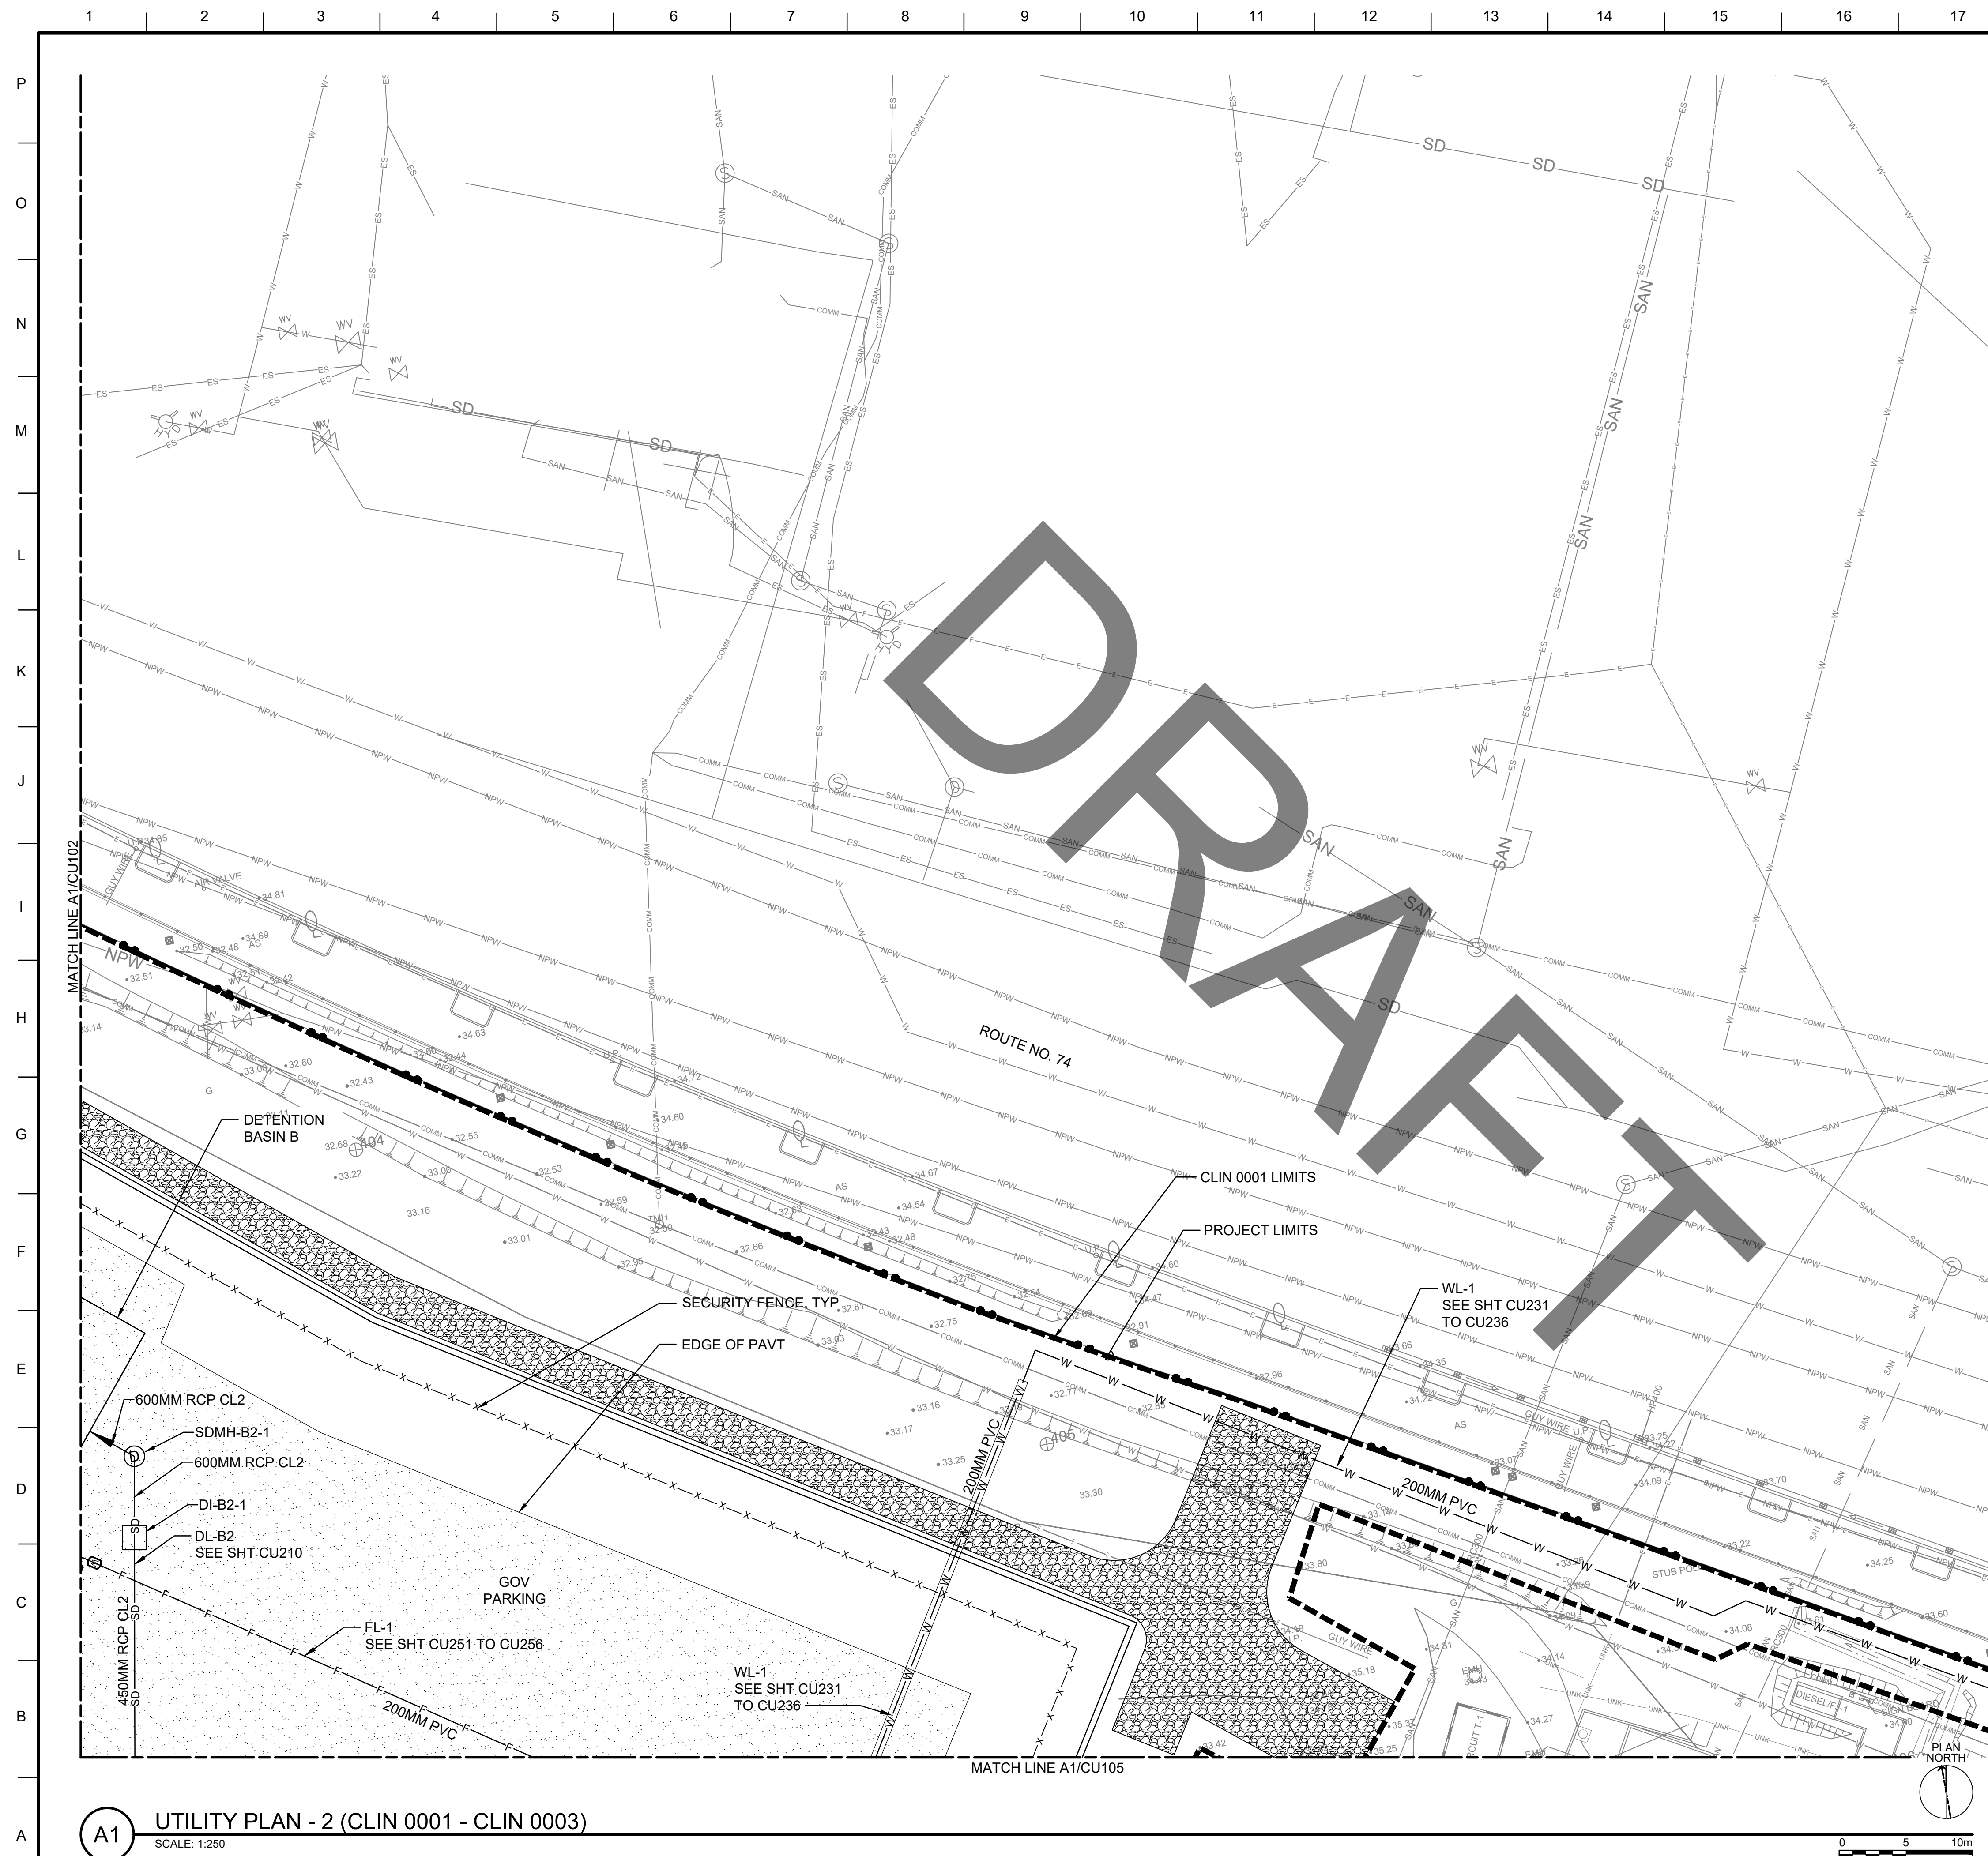

GENERAL NOTES

1. ALL DIMENSIONS SHOWN IN CALLOUT/NOTES ARE IN METERS UNLESS OTHERWISE NOTED.

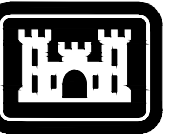

**US Army Corps
of Engineers®**

SHEET LEGEND

- | | |
|--|----------------|
| | PROJECT LIMITS |
| | SWALE |
| | DRAINLINE |
| | SEWERLINE |
| | WATERLINE |
| | FIRELINE |
| | DRAIN MANHOLE |
| | SEWER MANHOLE |
| | FIRE HYDRANT |

[illegible]


US ARMY CORPS OF ENGINEERS JAPAN DISTRICT, OKINAWA AREA OFFICE USAO-J, UNIT 35132 APO-JF 96374-1532		DESIGNED BY: DRAWN BY: SOLICITATION NO.: CHECKED BY: CONTRACT NO.: SCALE: AS SHOWN
 S&S INTERNATIONAL, INC. 501 SUMNER STREET, SUITE 620 HONOLULU, HAWAII 96817		SUBMITTED BY: FILE NAME: SIZE: ISO A1


KADENA AIR BASE, OKINAWA, JAPAN
VEHICLE MAINTENANCE SHOP
FY20 MCA PNT7833

03
ID
INTERMEDIATE DESIGN

CLIN 0001-0003

KEY PLAN

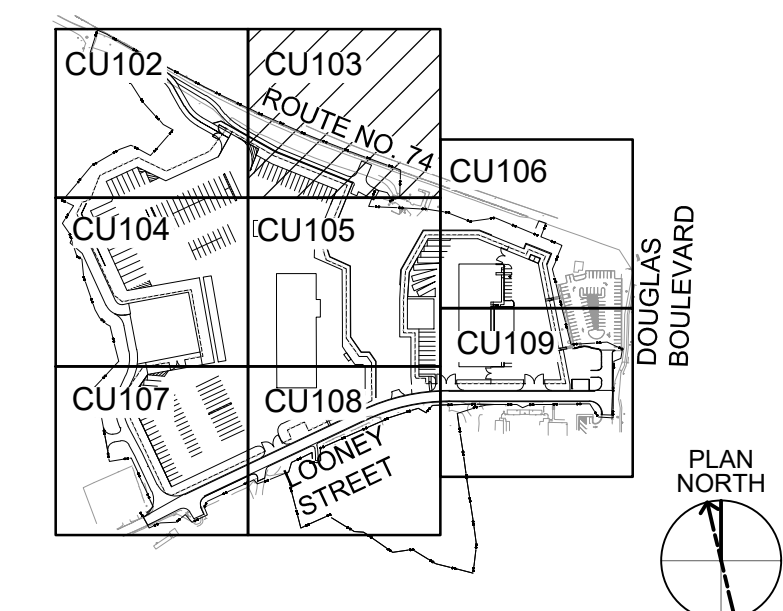

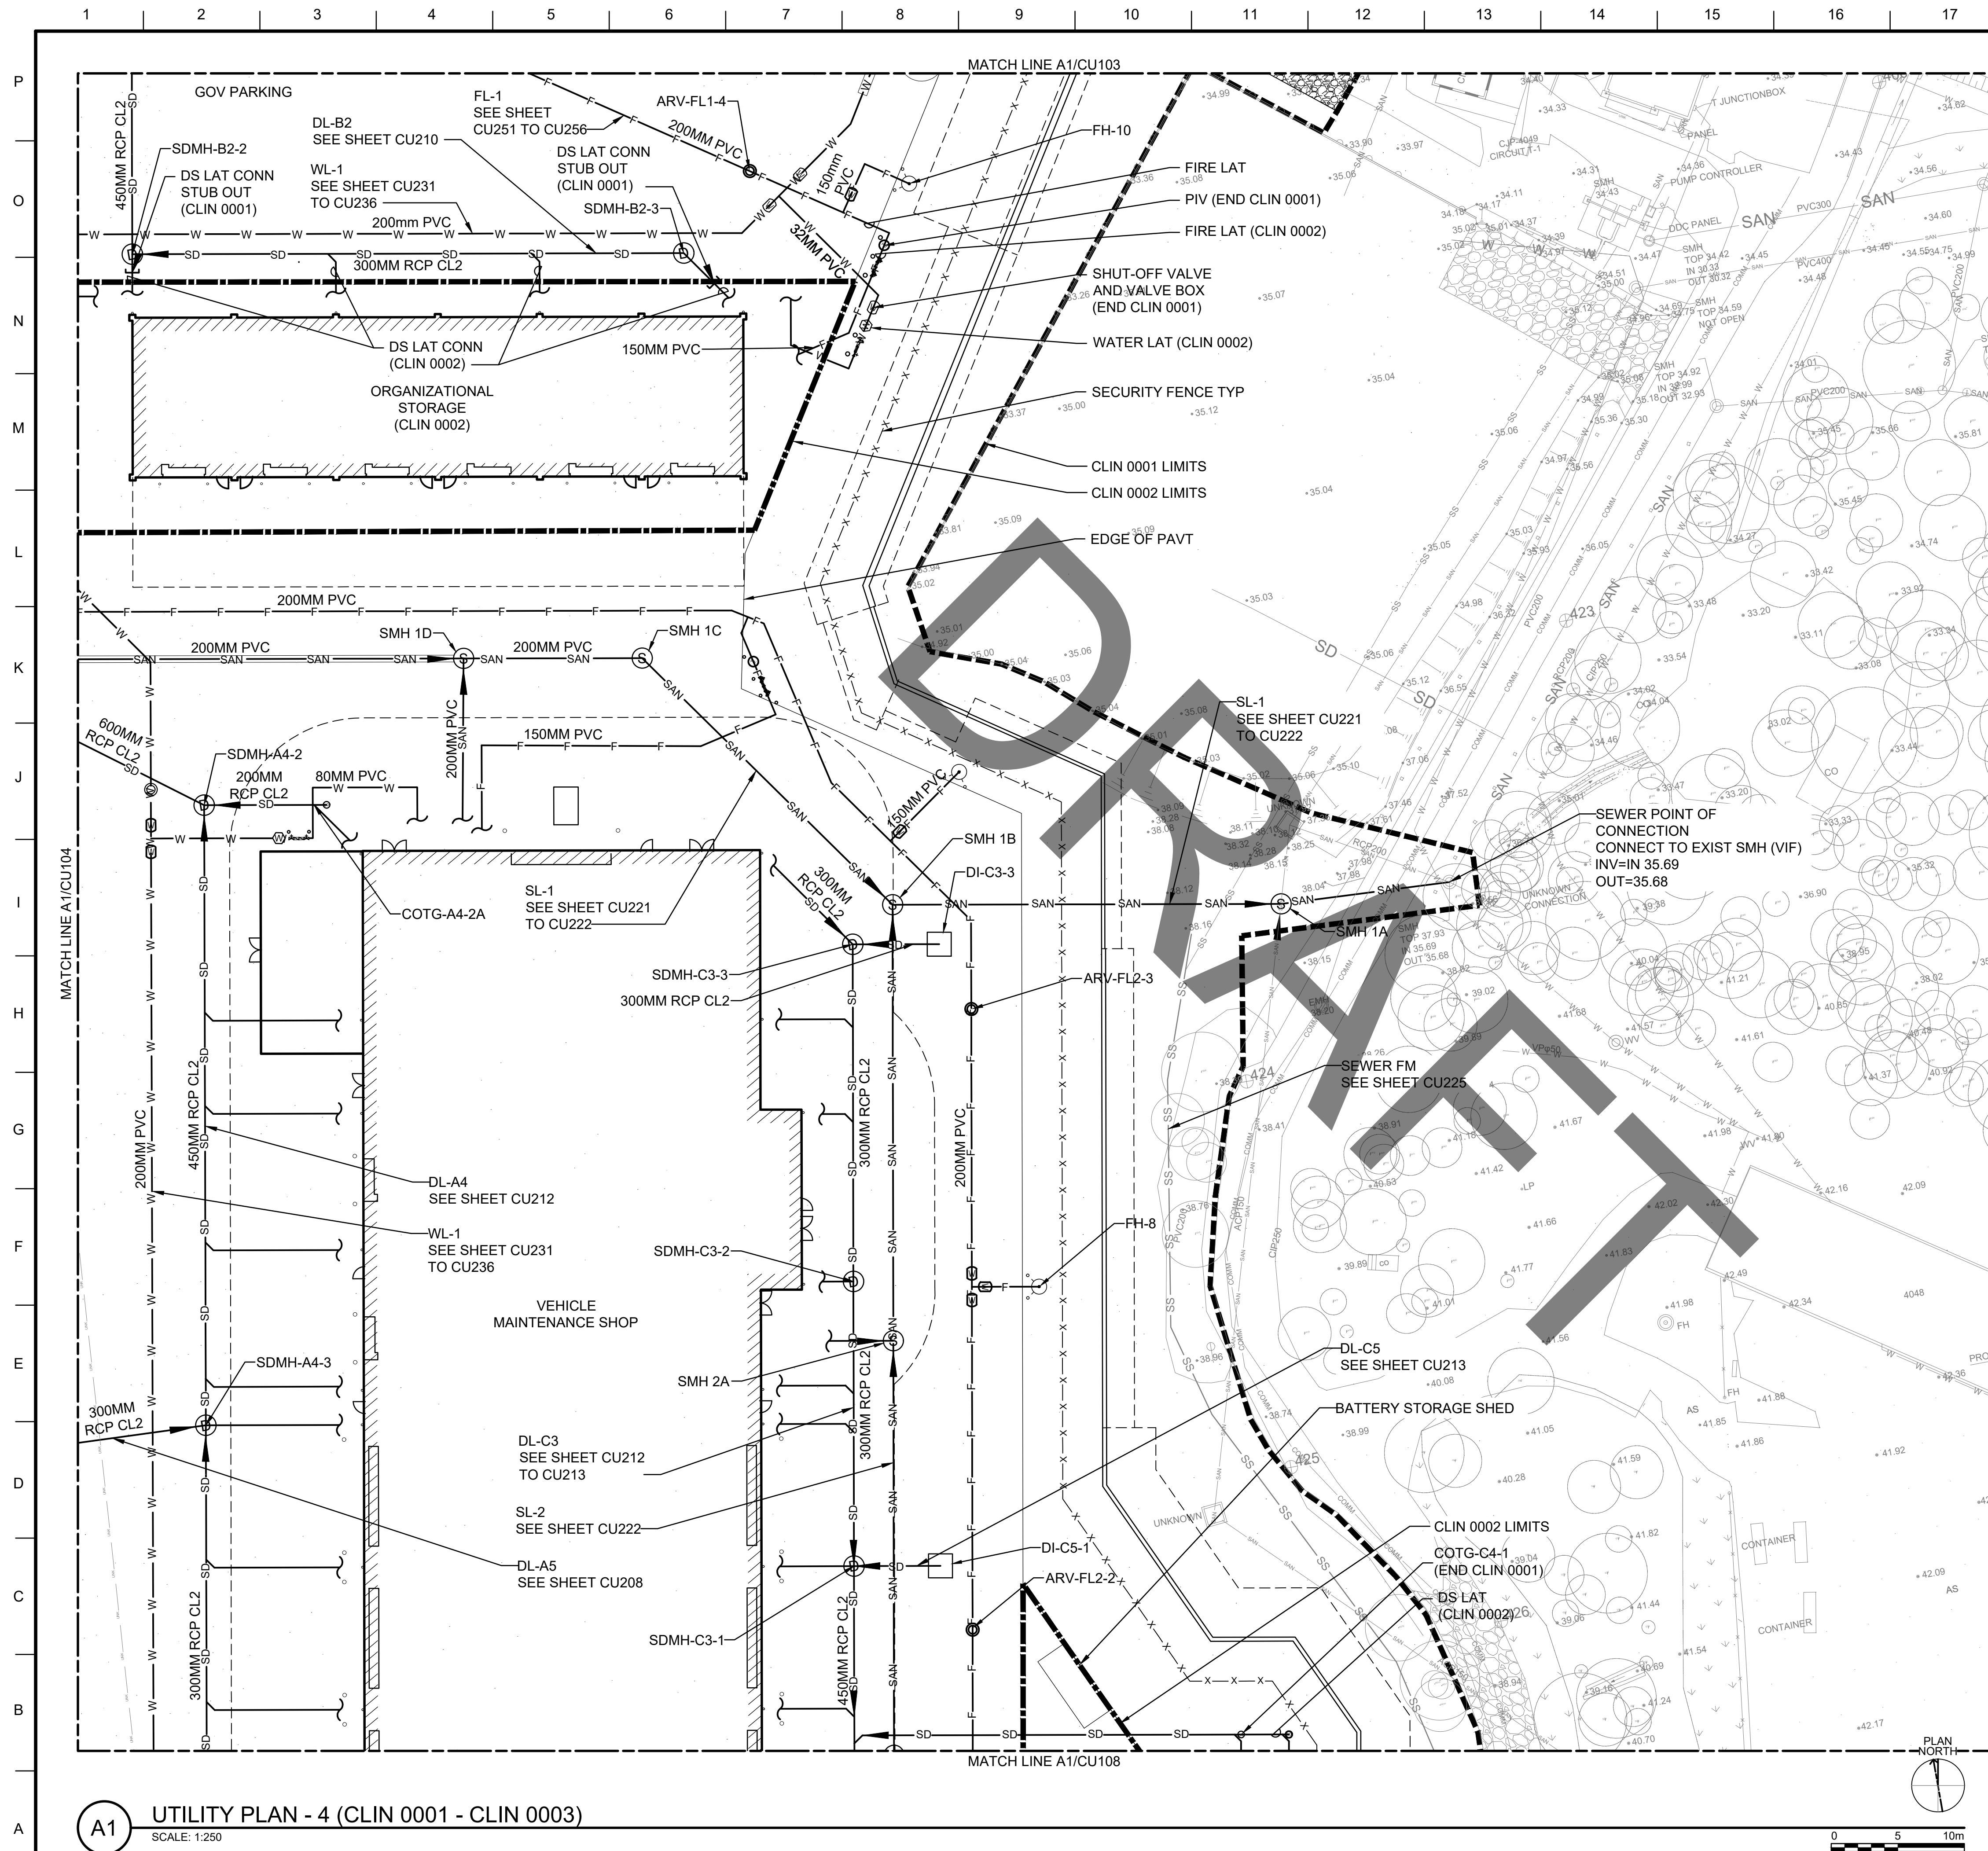

A1 UTILITY PLAN - 4 (CLIN 0001 - CLIN 0003)
SCALE: 1:250

GENERAL NOTES


1. ALL DIMENSIONS SHOWN IN CALLOUT/NOTES ARE IN METERS UNLESS OTHERWISE NOTED.

SHEET LEGEND

- PROJECT LIMITS
- SWALE
- DRAINLINE
- SEWERLINE
- WATERLINE
- FIRELINE
- DRAIN MANHOLE
- SEWER MANHOLE
- FIRE HYDRANT

CLIN 0001-0003

KEY PLAN

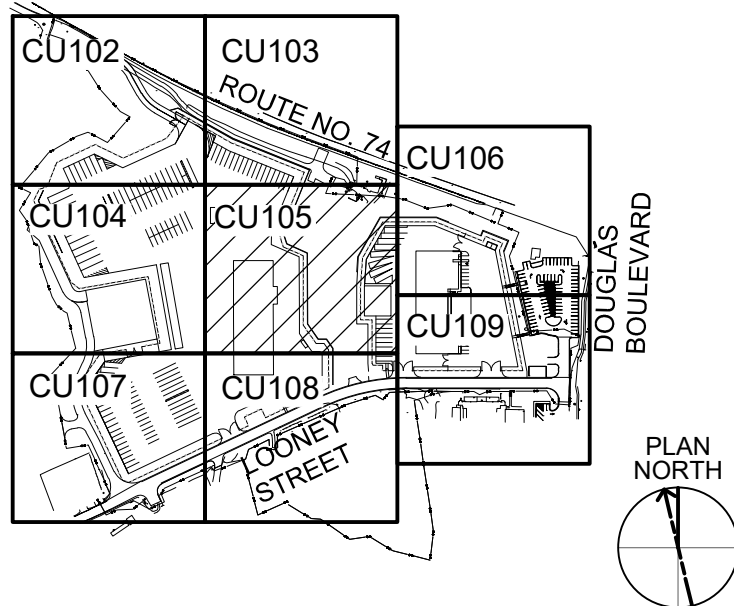

US Army Corps of Engineers®

ISSUE DATE:		SHEET ID	
DESIGNED BY:	ISSUE DATE:	CU105	DATE:
DRAWN BY:	SOLICITATION NO.:		
CHECKED BY:	CONTRACT NO.:		
SUBMITTED BY:	SCALE:		
FILE NAME:	AS SHOWN		

US ARMY CORPS OF ENGINEERS
JAPAN DISTRICT, OKINAWA AREA OFFICE
USAFED-J UNIT 35132
APO AP 96374-5132

SSFM
SSFM INTERNATIONAL, INC.
501 SUMNER STREET, SUITE 620
HONOLULU, HAWAII 96817

KADENA AIR BASE, OKINAWA, JAPAN
VEHICLE MAINTENANCE SHOP
FY20 MCA PN77833

UTILITY PLAN - 4 (CLIN 0001 - CLIN 0003)

SHEET ID

CU105

INTERMEDIATE DESIGN



GENERAL NOTES


1. ALL DIMENSIONS SHOWN IN CALLOUT/NOTES ARE IN METERS UNLESS OTHERWISE NOTED.

SHEET LEGEND

- PROJECT LIMITS
- SWALE
- DRAINLINE
- SAN SEWERLINE
- W WATERLINE
- F FIRELINE
- ⊙ DRAIN MANHOLE
- ⊙ SEWER MANHOLE
- ⊙ FIRE HYDRANT

CLIN 0001-0003

KEY PLAN

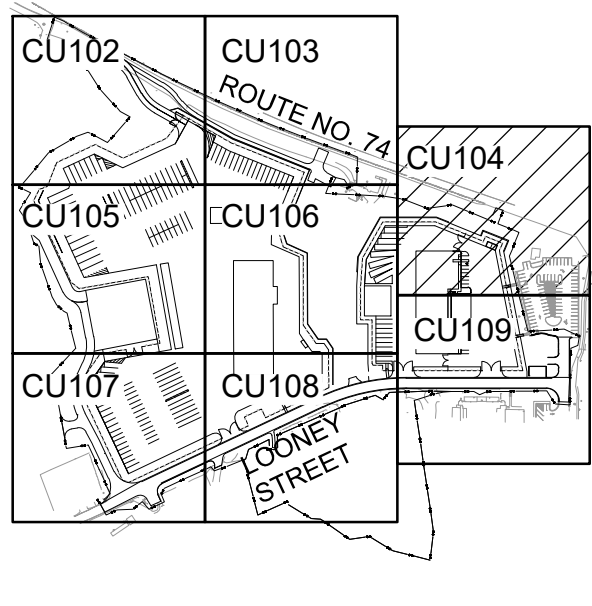

US Army Corps of Engineers

ISSUE DATE:		SHEET ID	
DESIGNED BY:	ISSUE DATE:	CU106	DATE
DRAWN BY:	SOLICITATION NO.:		
CHECKED BY:	CONTRACT NO.:		
SUBMITTED BY:	SCALE:		
FILE NAME:	AS SHOWN		

US ARMY CORPS OF ENGINEERS
JAPAN DISTRICT, OKINAWA AREA OFFICE
USAFED-J UNIT 35132
APO AP 96374-5132

SSM
SSM INTERNATIONAL, INC.
501 SUMNER STREET, SUITE 620
HONOLULU, HAWAII 96817


KADENA AIR BASE, OKINAWA, JAPAN
VEHICLE MAINTENANCE SHOP
FY20 MCA PN77833

UTILITY PLAN - 5 (CLIN 0001 - CLIN 0003)

SHEET ID


CU106

INTERMEDIATE DESIGN

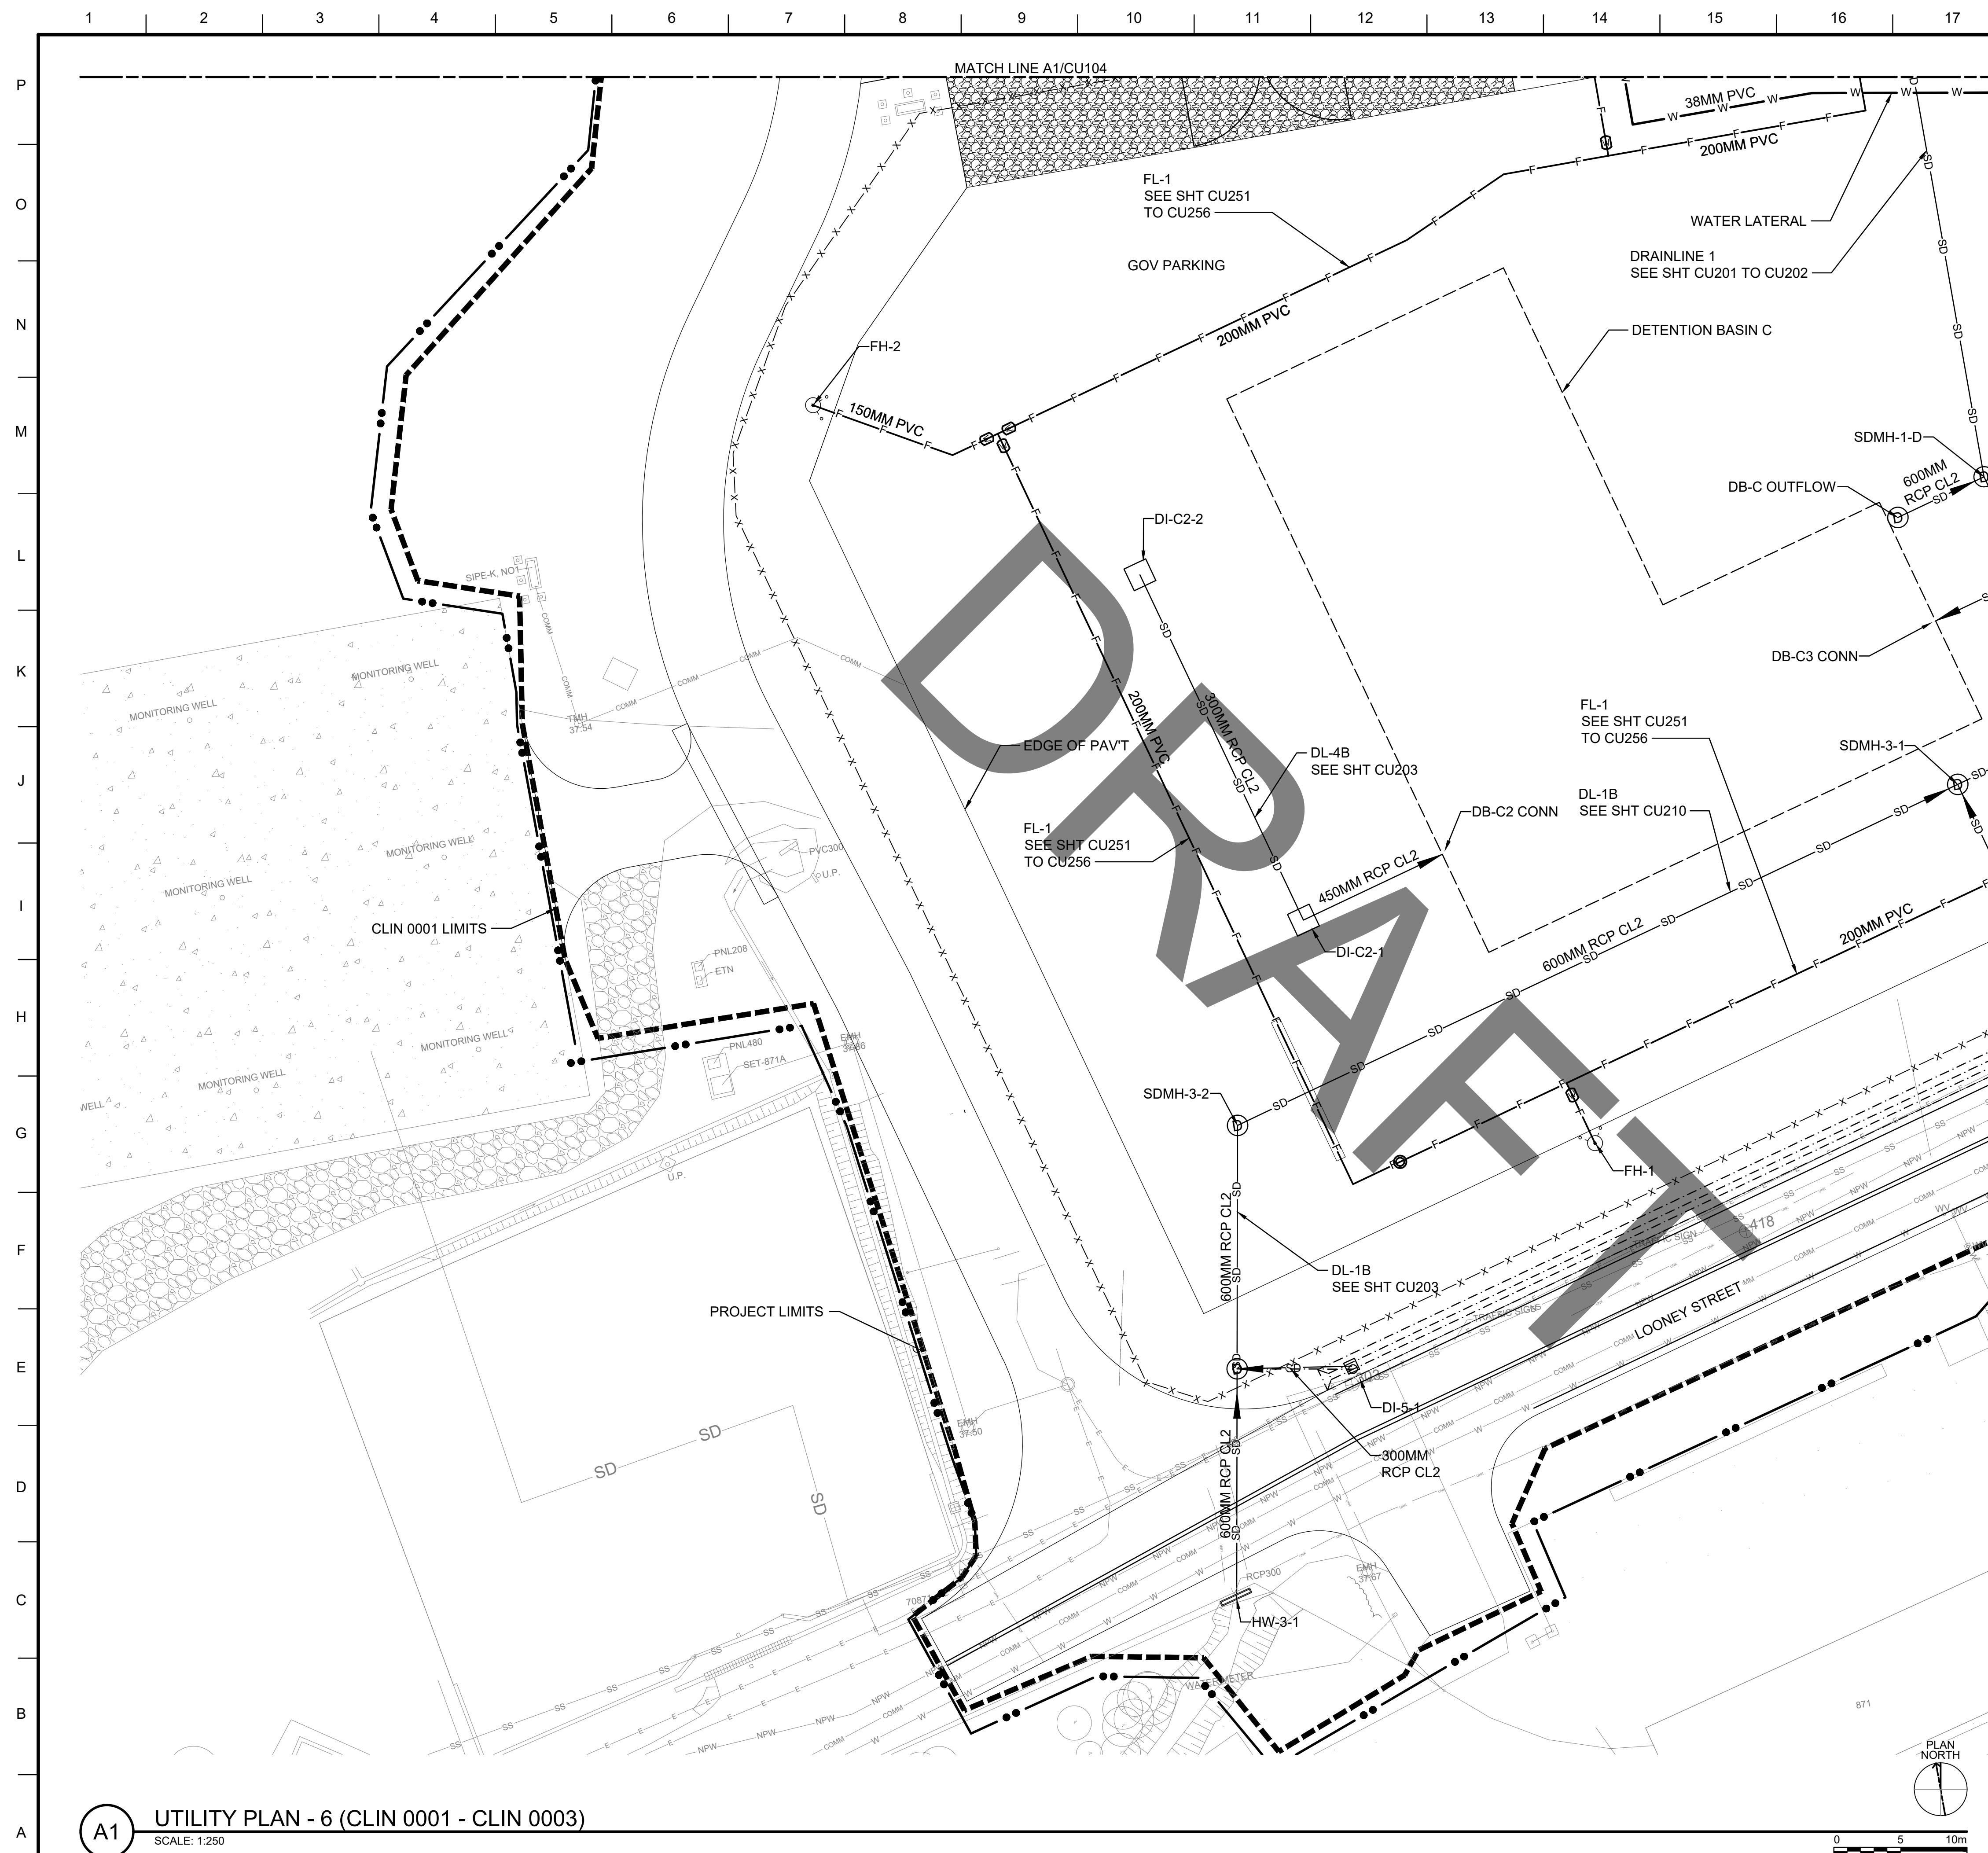

GENERAL NOTES

1. ALL DIMENSIONS SHOWN IN CALLOUT/NOTES ARE IN METERS
UNLESS OTHERWISE NOTED.

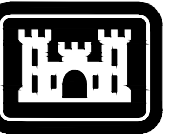

US Army Corps
of Engineers®

[illegible]

SHEET LEGEND

	PROJECT LIMITS
	SWALE
	DRAINLINE
	SEWERLINE
	WATERLINE
	FIRELINE
	DRAIN MANHOLE
	SEWER MANHOLE
	FIRE HYDRANT

JAPAN DISTRICT OKINAWA AREA OFFICE USAED-1 UNIT 35132 APO, AP 96374-5132	DRAWN BY:		SOLICITATION NO.:
	CHECKED BY:		CONTRACT NO.:
 SSFM INTERNATIONAL, INC. 501 SUMNER STREET, SUITE 620 HONOLULU, HAWAII 96817	SUBMITTED BY:		SCALE: AS SHOWN
	SIZE: US A1	FILE NAME:	


VEHICLE MAINTENANCE SHOP
FY20 MCA PN77833

UTILITY PLAN - 6 (CLIN 0001 - CLIN 0003)


SHEET ID

CU107

KEY PLAN

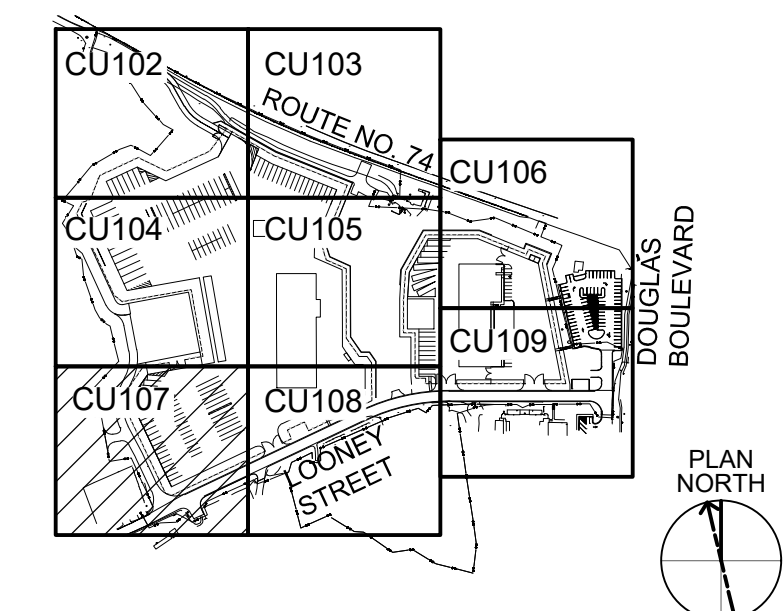

INTERMEDIATE DESIGN

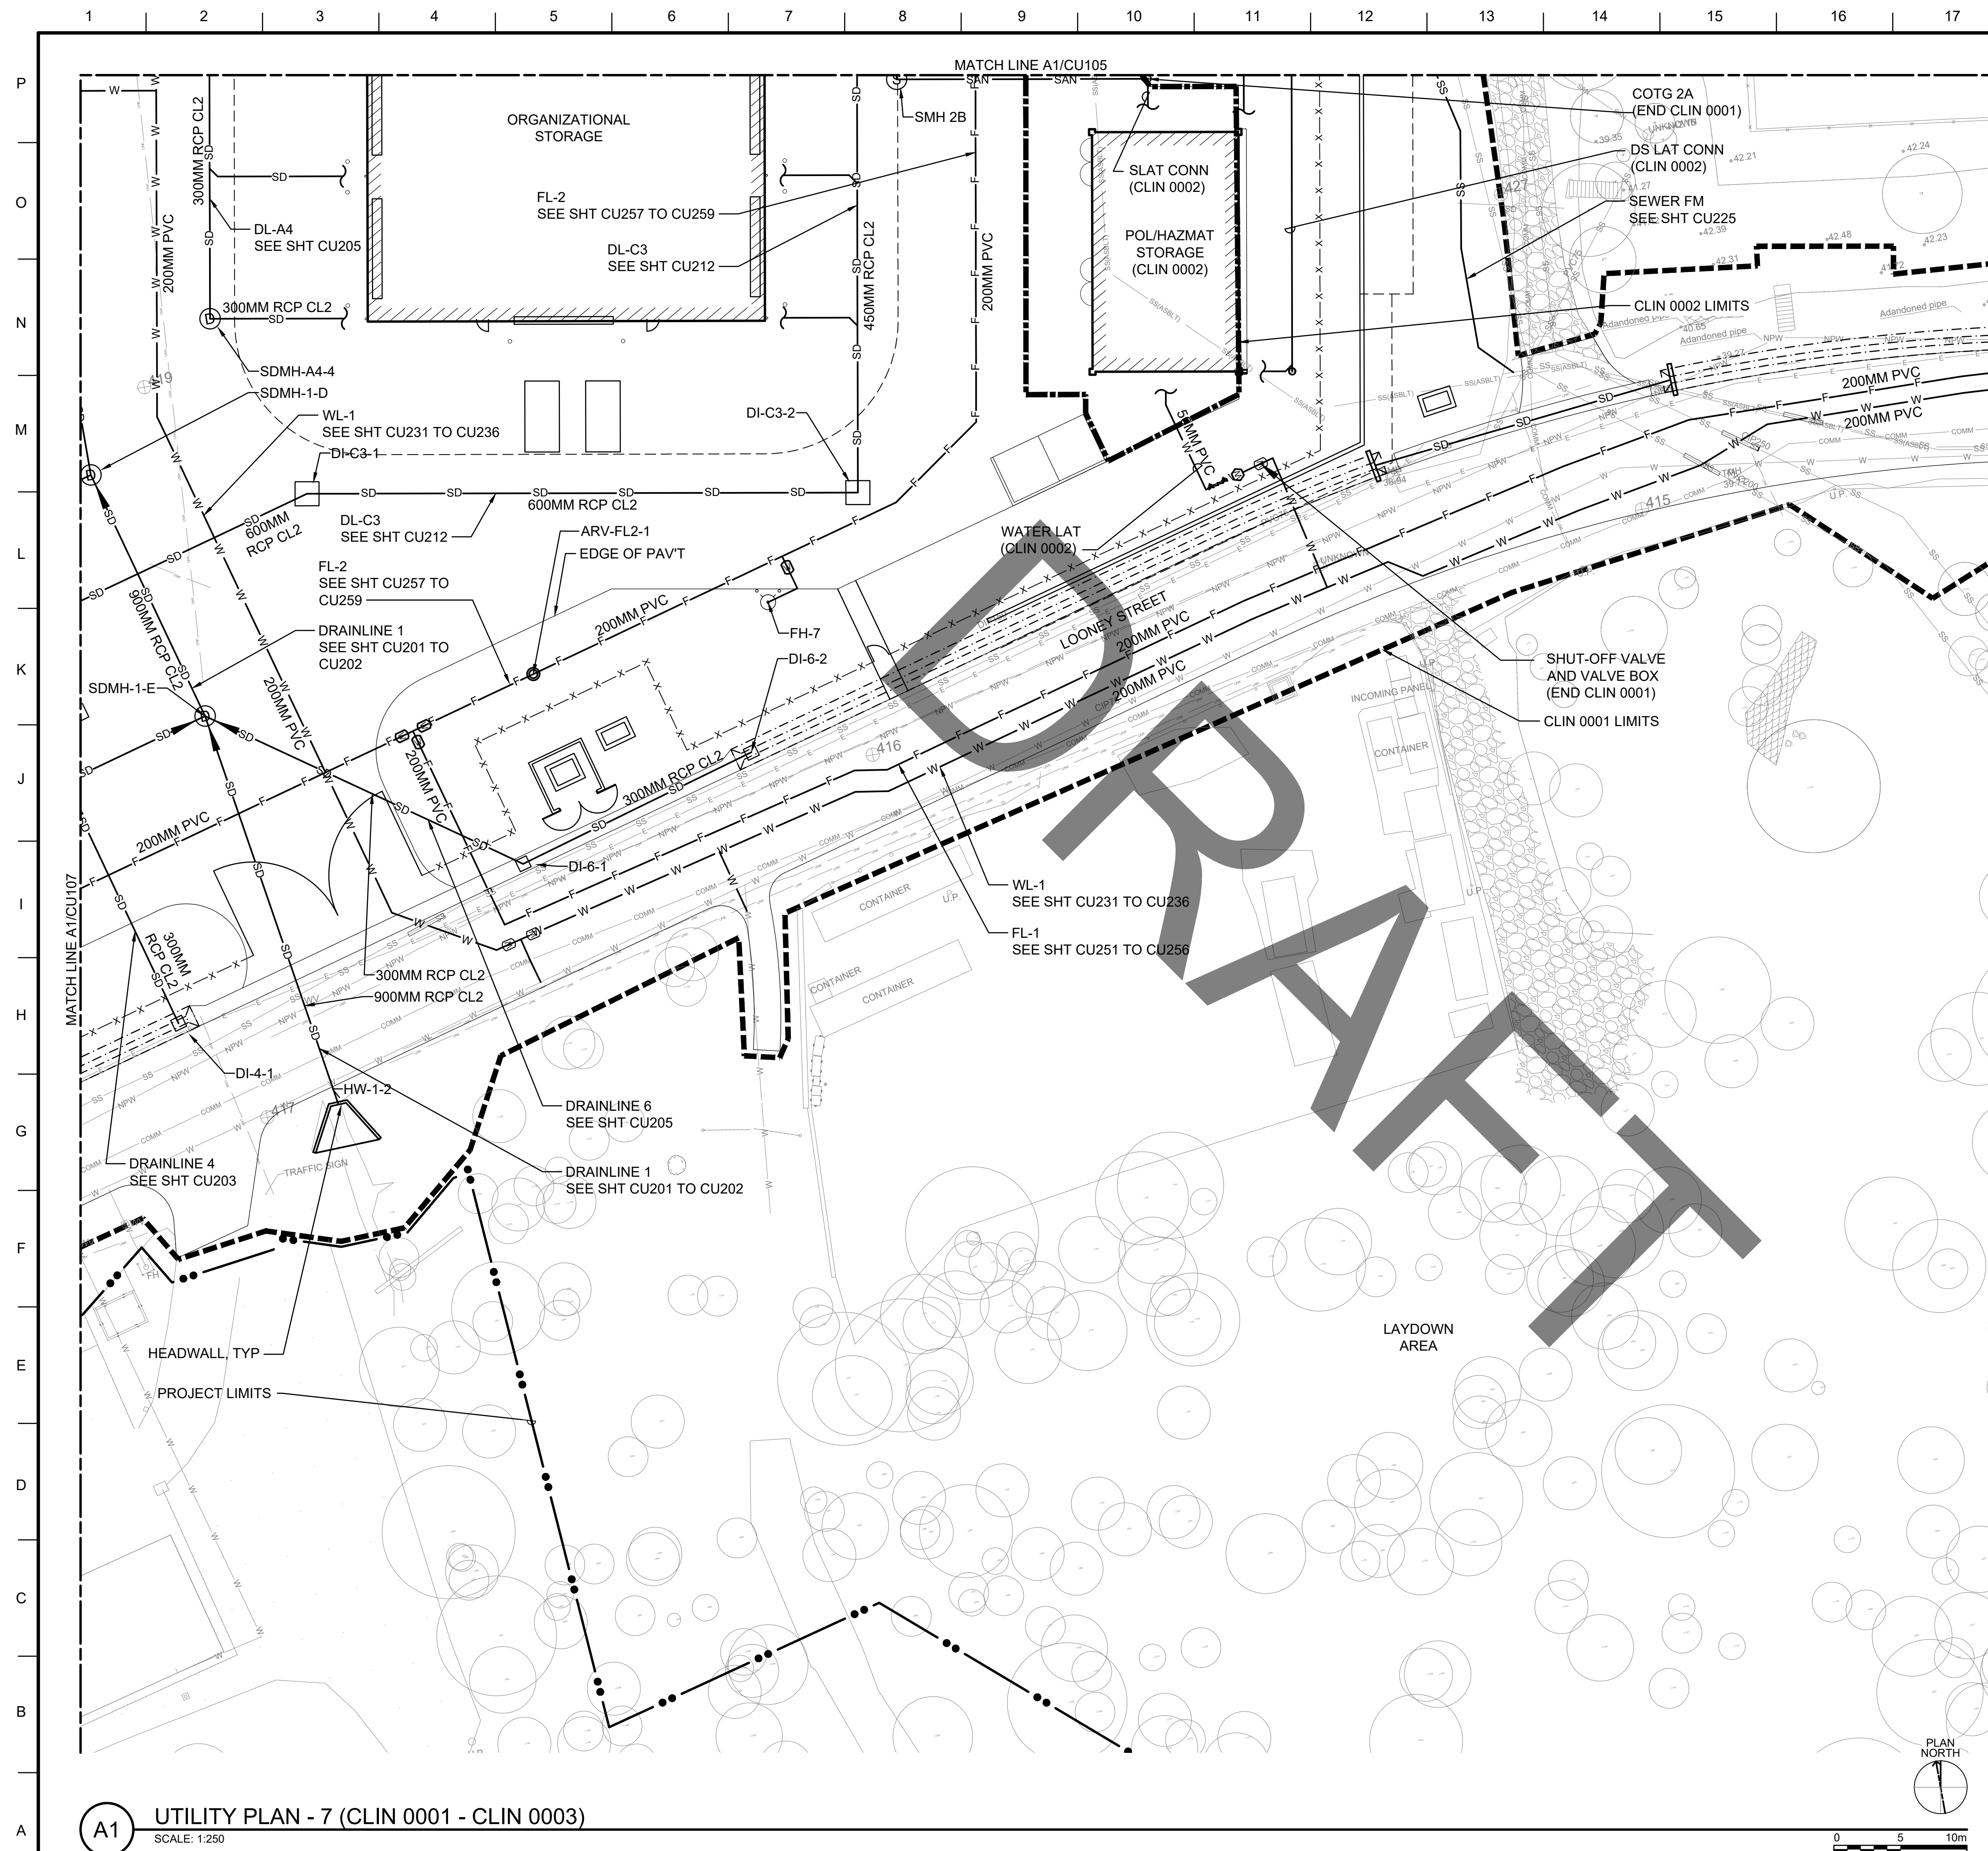


GENERAL NOTES

1. ALL DIMENSIONS SHOWN IN CALLOUT/NOTES ARE IN METERS
UNLESS OTHERWISE NOTED.




US Army Corps
of Engineers®

SHEET LEGEND

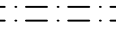	PROJECT LIMITS
	SWALE
	DRAINLINE
	SEWERLINE
	WATERLINE
	FIRELINE
	DRAIN MANHOLE
	SEWER MANHOLE
	FIRE HYDRANT

KEY PLAN

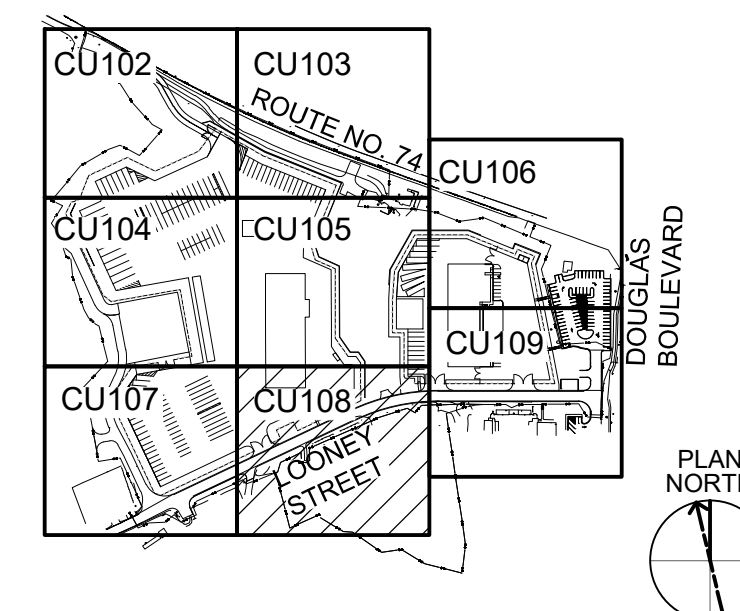


ISSUE DATE:	CONTRACT N°:	SCALE: AS SHOWN
SOLICITATION:	CHECKED BY:	SUBMITTED BY:
DESIGNED BY:	DRAWN BY:	SIZE: FILE NAME:
DISTRICT, OKINAWA AREA OFFICE U.S. ARMY CORPS OF ENGINEERS USED-J, UNIT 35132 APO, AP 96374-5132  SSFM INTERNATIONAL, INC SUMMER STREET, SUITE 620		

KADENA AIR BASE, OKINAWA, JAPAN
VEHICLE MAINTENANCE SHOP
FY20 MCA PN77833

SHEET ID


CU10

INTERMEDIATE DESIGN

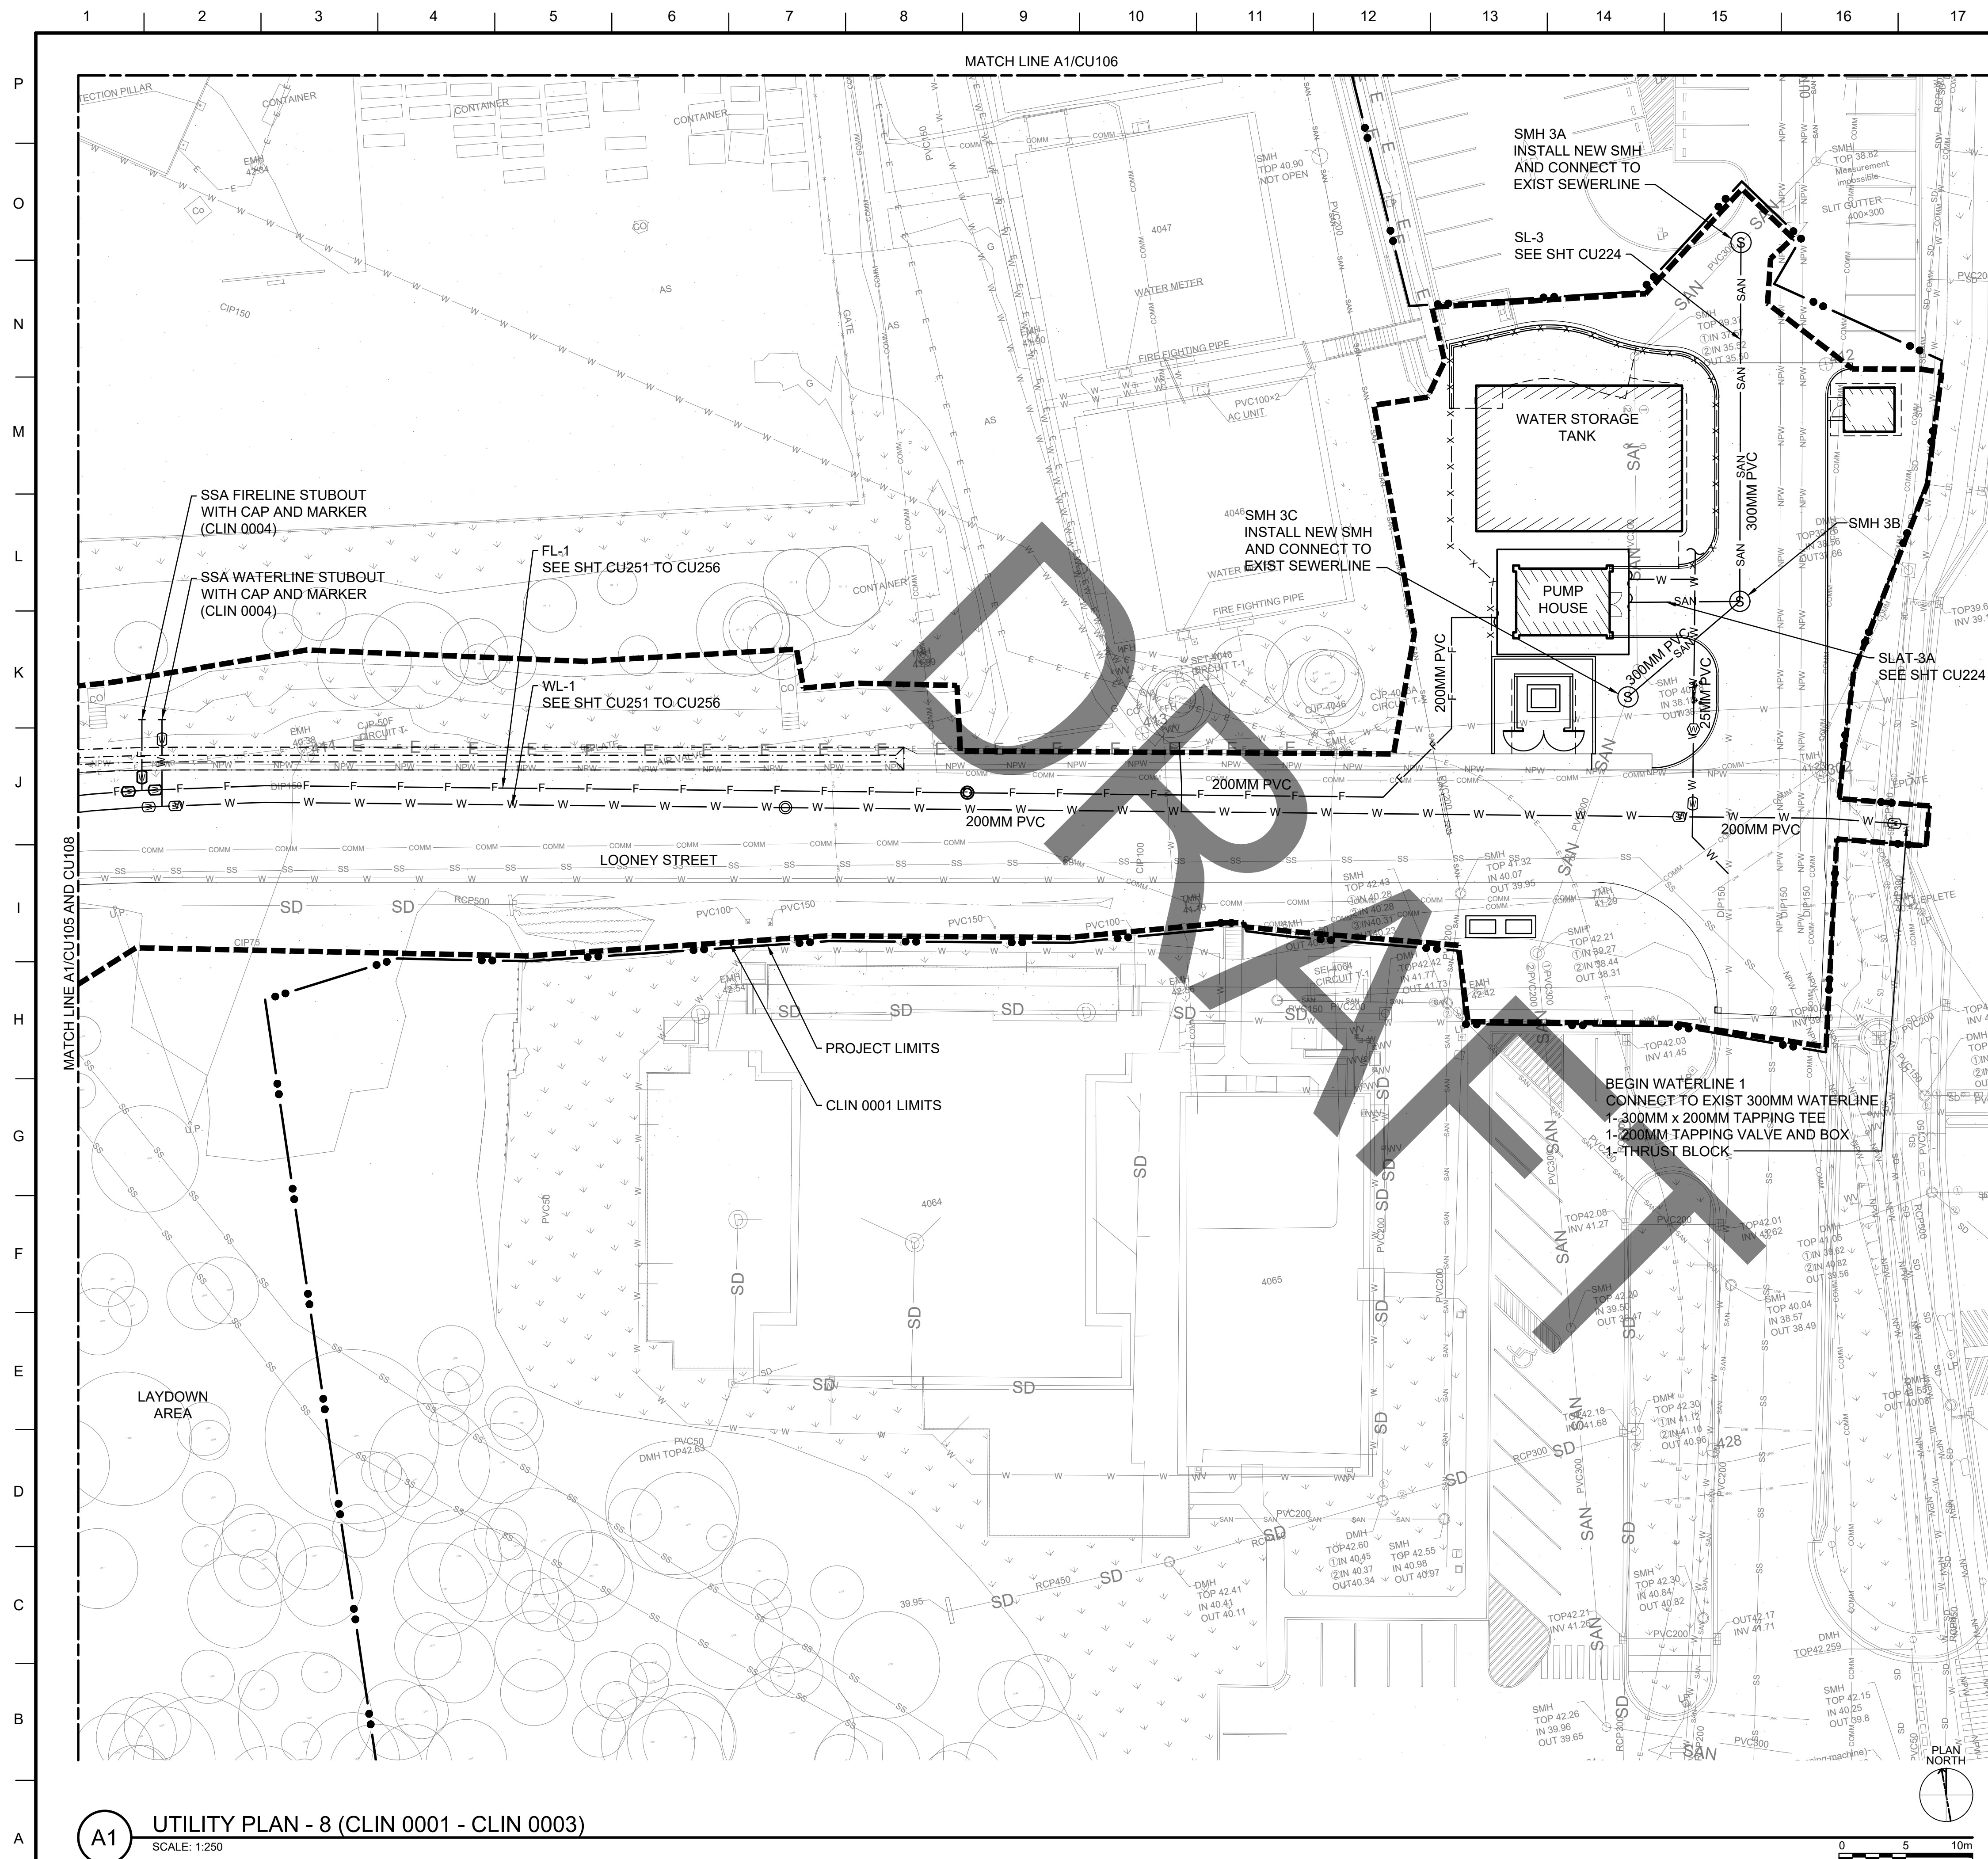


GENERAL NOTES

1. ALL DIMENSIONS SHOWN IN CALLOUT/NOTES ARE IN METERS
UNLESS OTHERWISE NOTED.

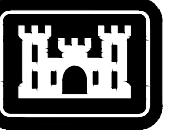

**US Army Corps
of Engineers®**

SHEET LEGEND

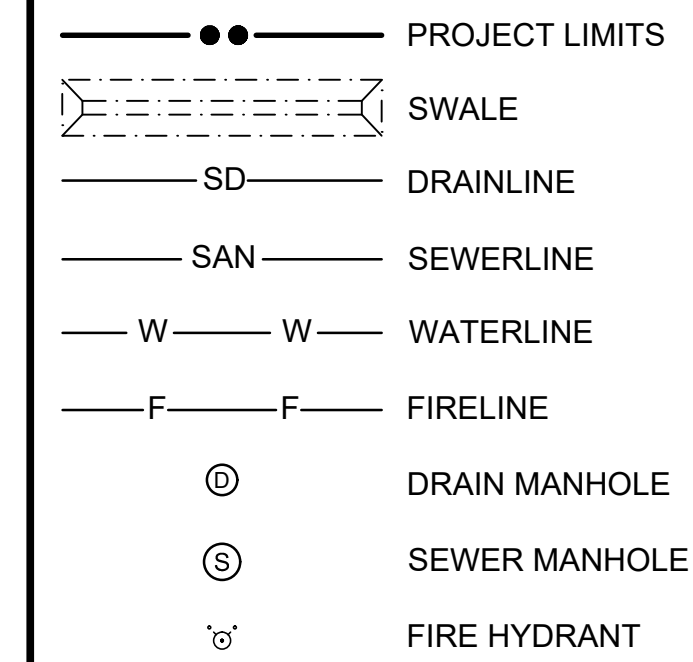

DRAWN BY:	SOLICITATION
CHECKED BY:	CONTRACT N
SUBMITTED BY:	SCALE: AS SHOWN
SIZE: ISO A1	FILE NAME:

JAPAN DISTRICT, OKINAWA AREA OFFICE
USAFED-I, UNIT 35132
APO, AP 96374-5132


SSFM
International
SSFM INTERNATIONAL, INC
501 SUMNER STREET, SUITE 620
HONOLULU, HAWAII 96817

UTILITY PLAN - 8 (CLIN 0001 - CLIN 0003)


SHEET ID

CU109

KEY PLAN

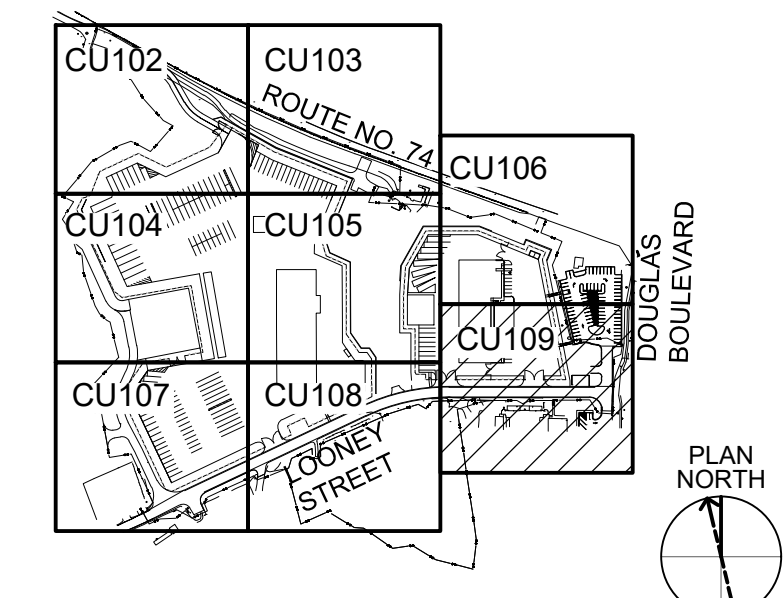

INTERMEDIATE DESIGN

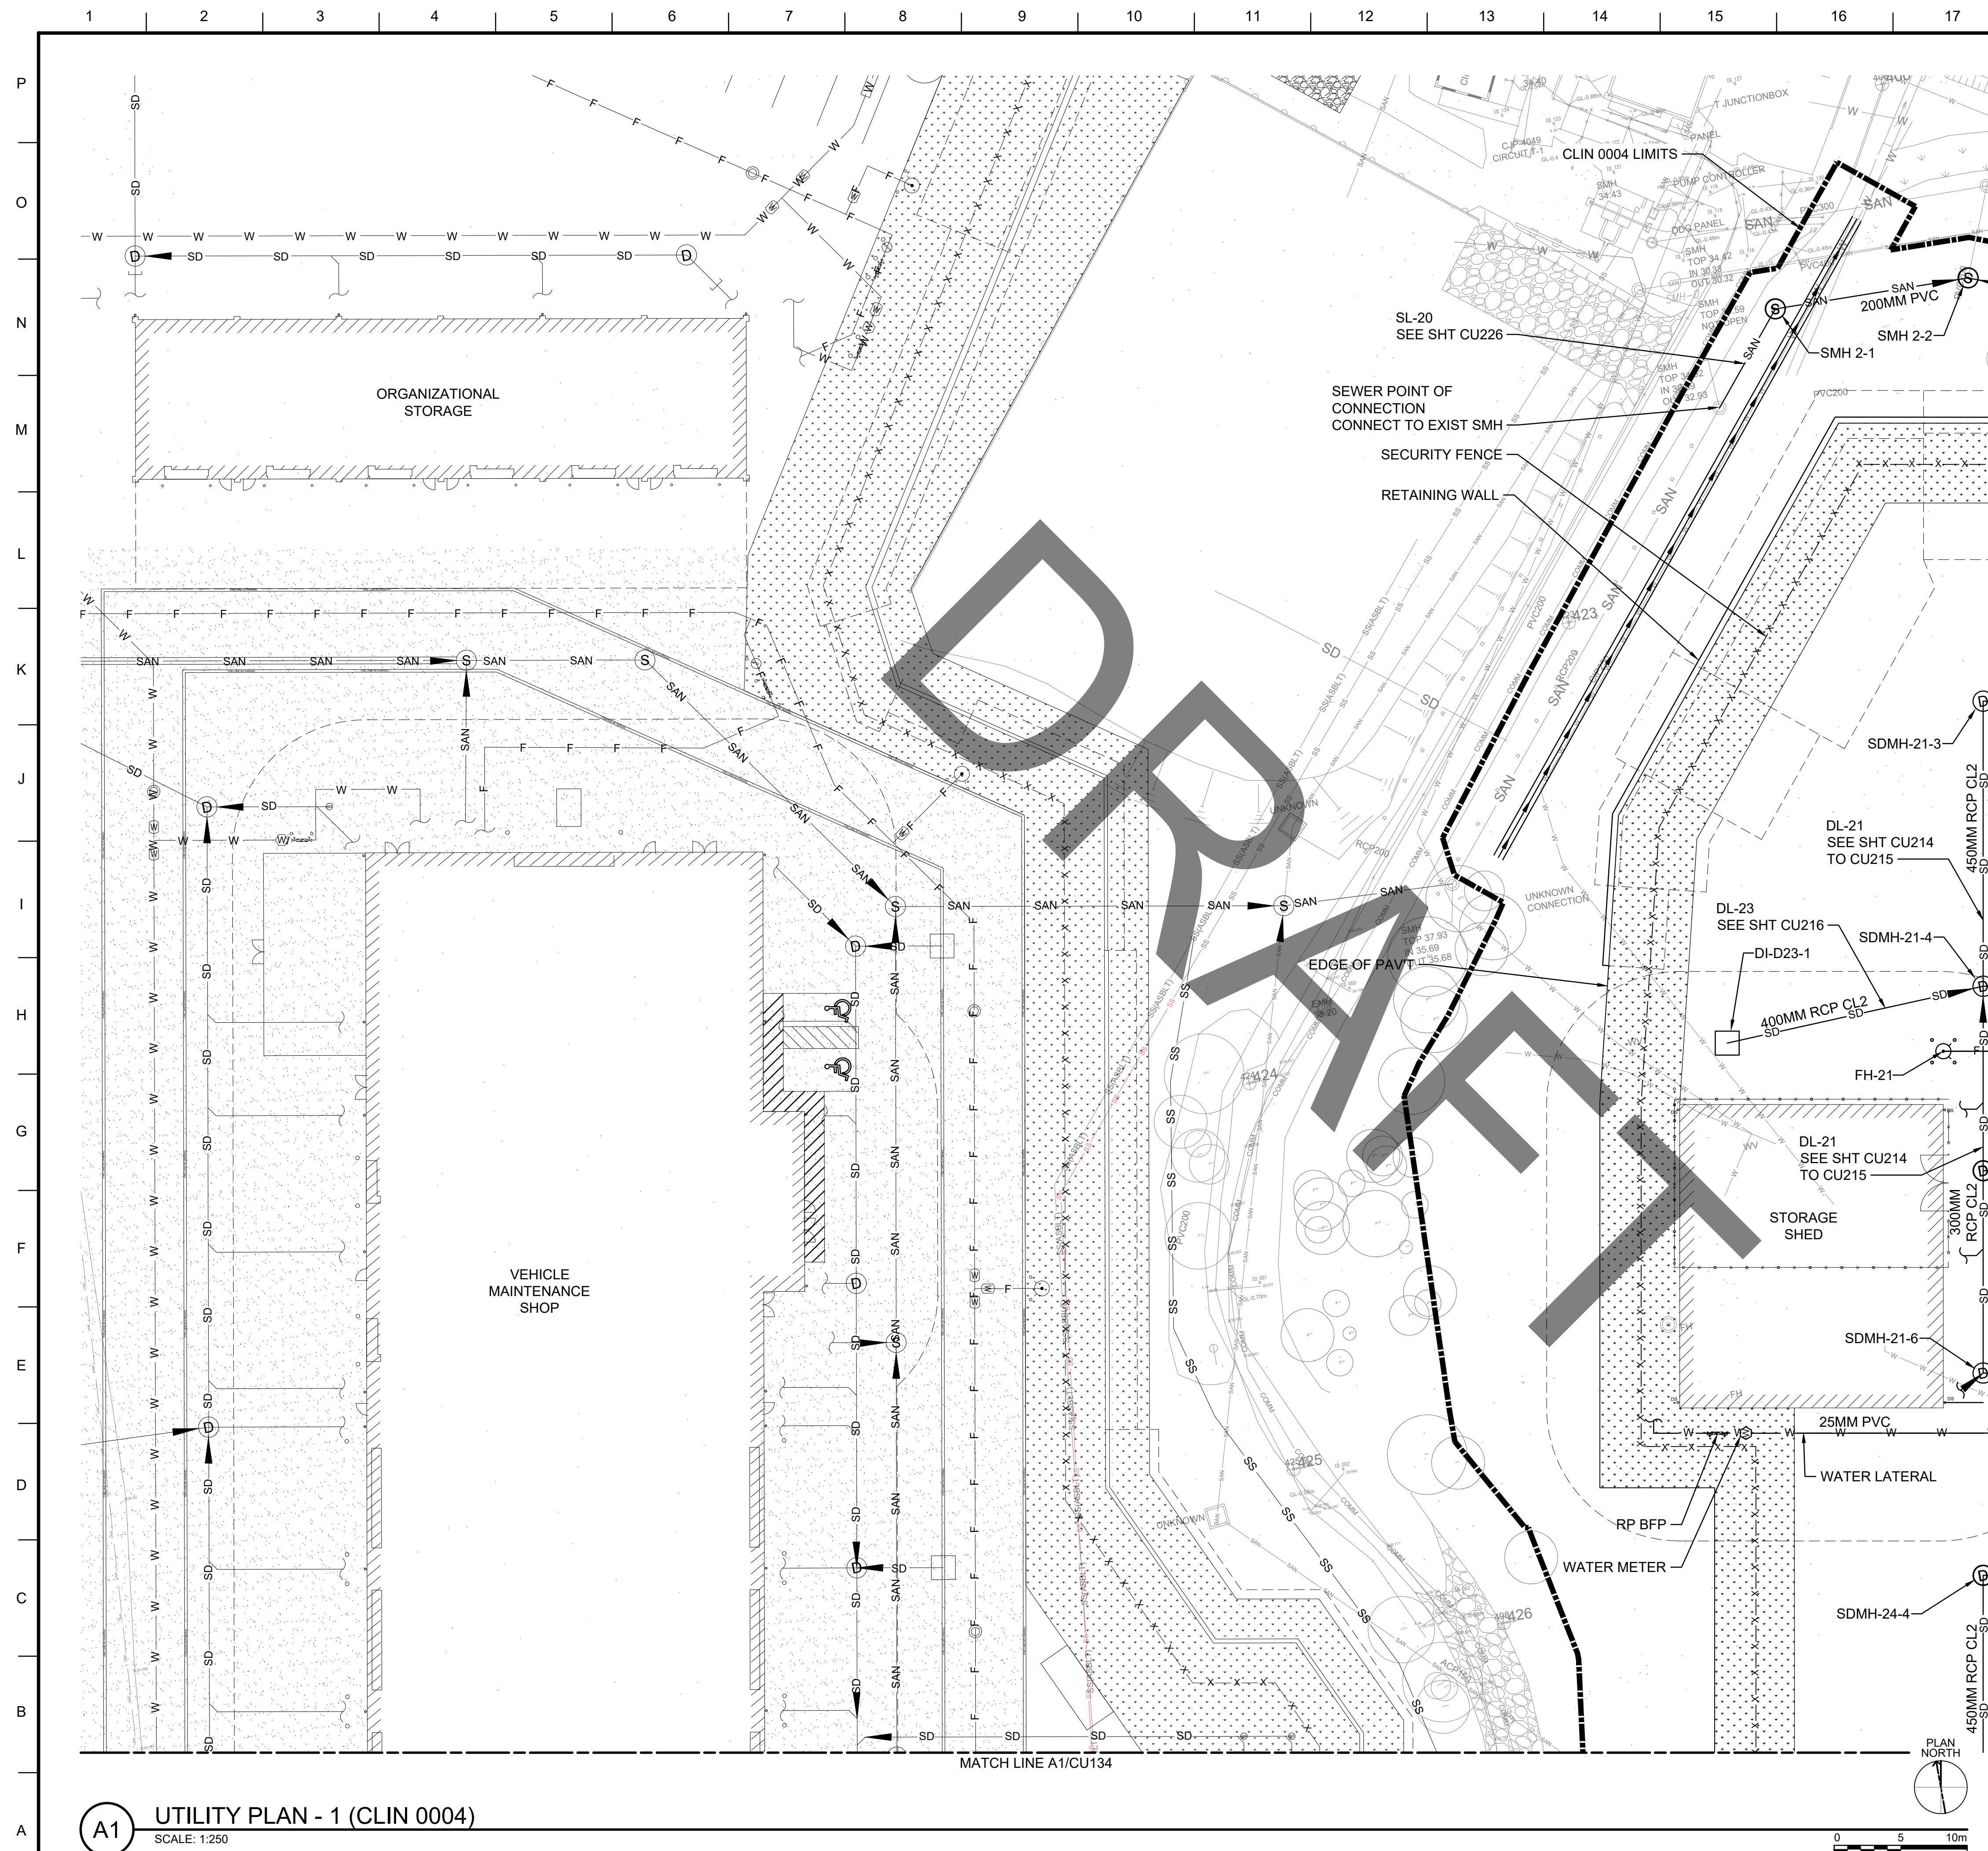

GENERAL NOTES



**U.S. Army Corps
Engineers®**

[illegible]

DRAWN BY: USAED-J, UNIT 35132 APO, AP 96374-5132	SOLUTION NO.:
CHECKED BY:	CONTRACT NO.:
SUBMITTED BY:	SCALE: AS SHOWN
SIZE:	FILE NAME:
ISO A1	ISO A1



SSPM
 INTERNATIONAL, INC.
 501 SUMNER STREET, SUITE 620
 HONOLULU, HAWAII 96817

FY20 MCA PN77833

UTILITY PLAN - 1 (CLIN 0004)


SHEET ID
CU132

SHEET LEGEND


	PROJECT LIMITS
	SWALE
	DRAINLINE
	SEWERLINE
	WATERLINE
	FIRELINE
	DRAIN MANHOLE
	SEWER MANHOLE
	FIRE HYDRANT

CLIN 0004:
TEMPORARY FACILITIES (COF SS)
DEMOLITION OF 8 EXISTING BUILDINGS
SITE PREPARATION, FENCING, AND
CLEARING OF SSA
SUPPLY SUPPORT ACTIVITY (SSA)
WAREHOUSE STORAGE SHED FOR SSA
PARKING AND PAVING FOR SSA


KEY PLAN

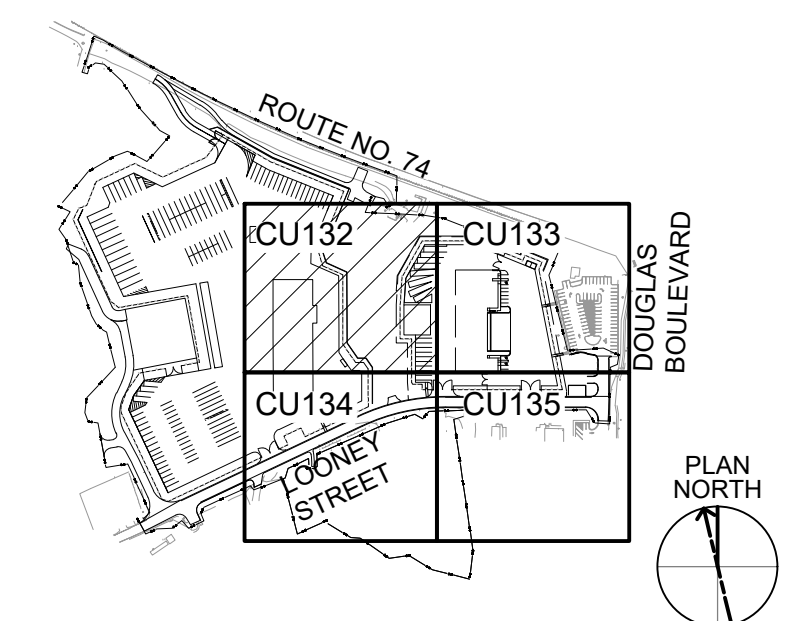

INTERMEDIATE DESIGN

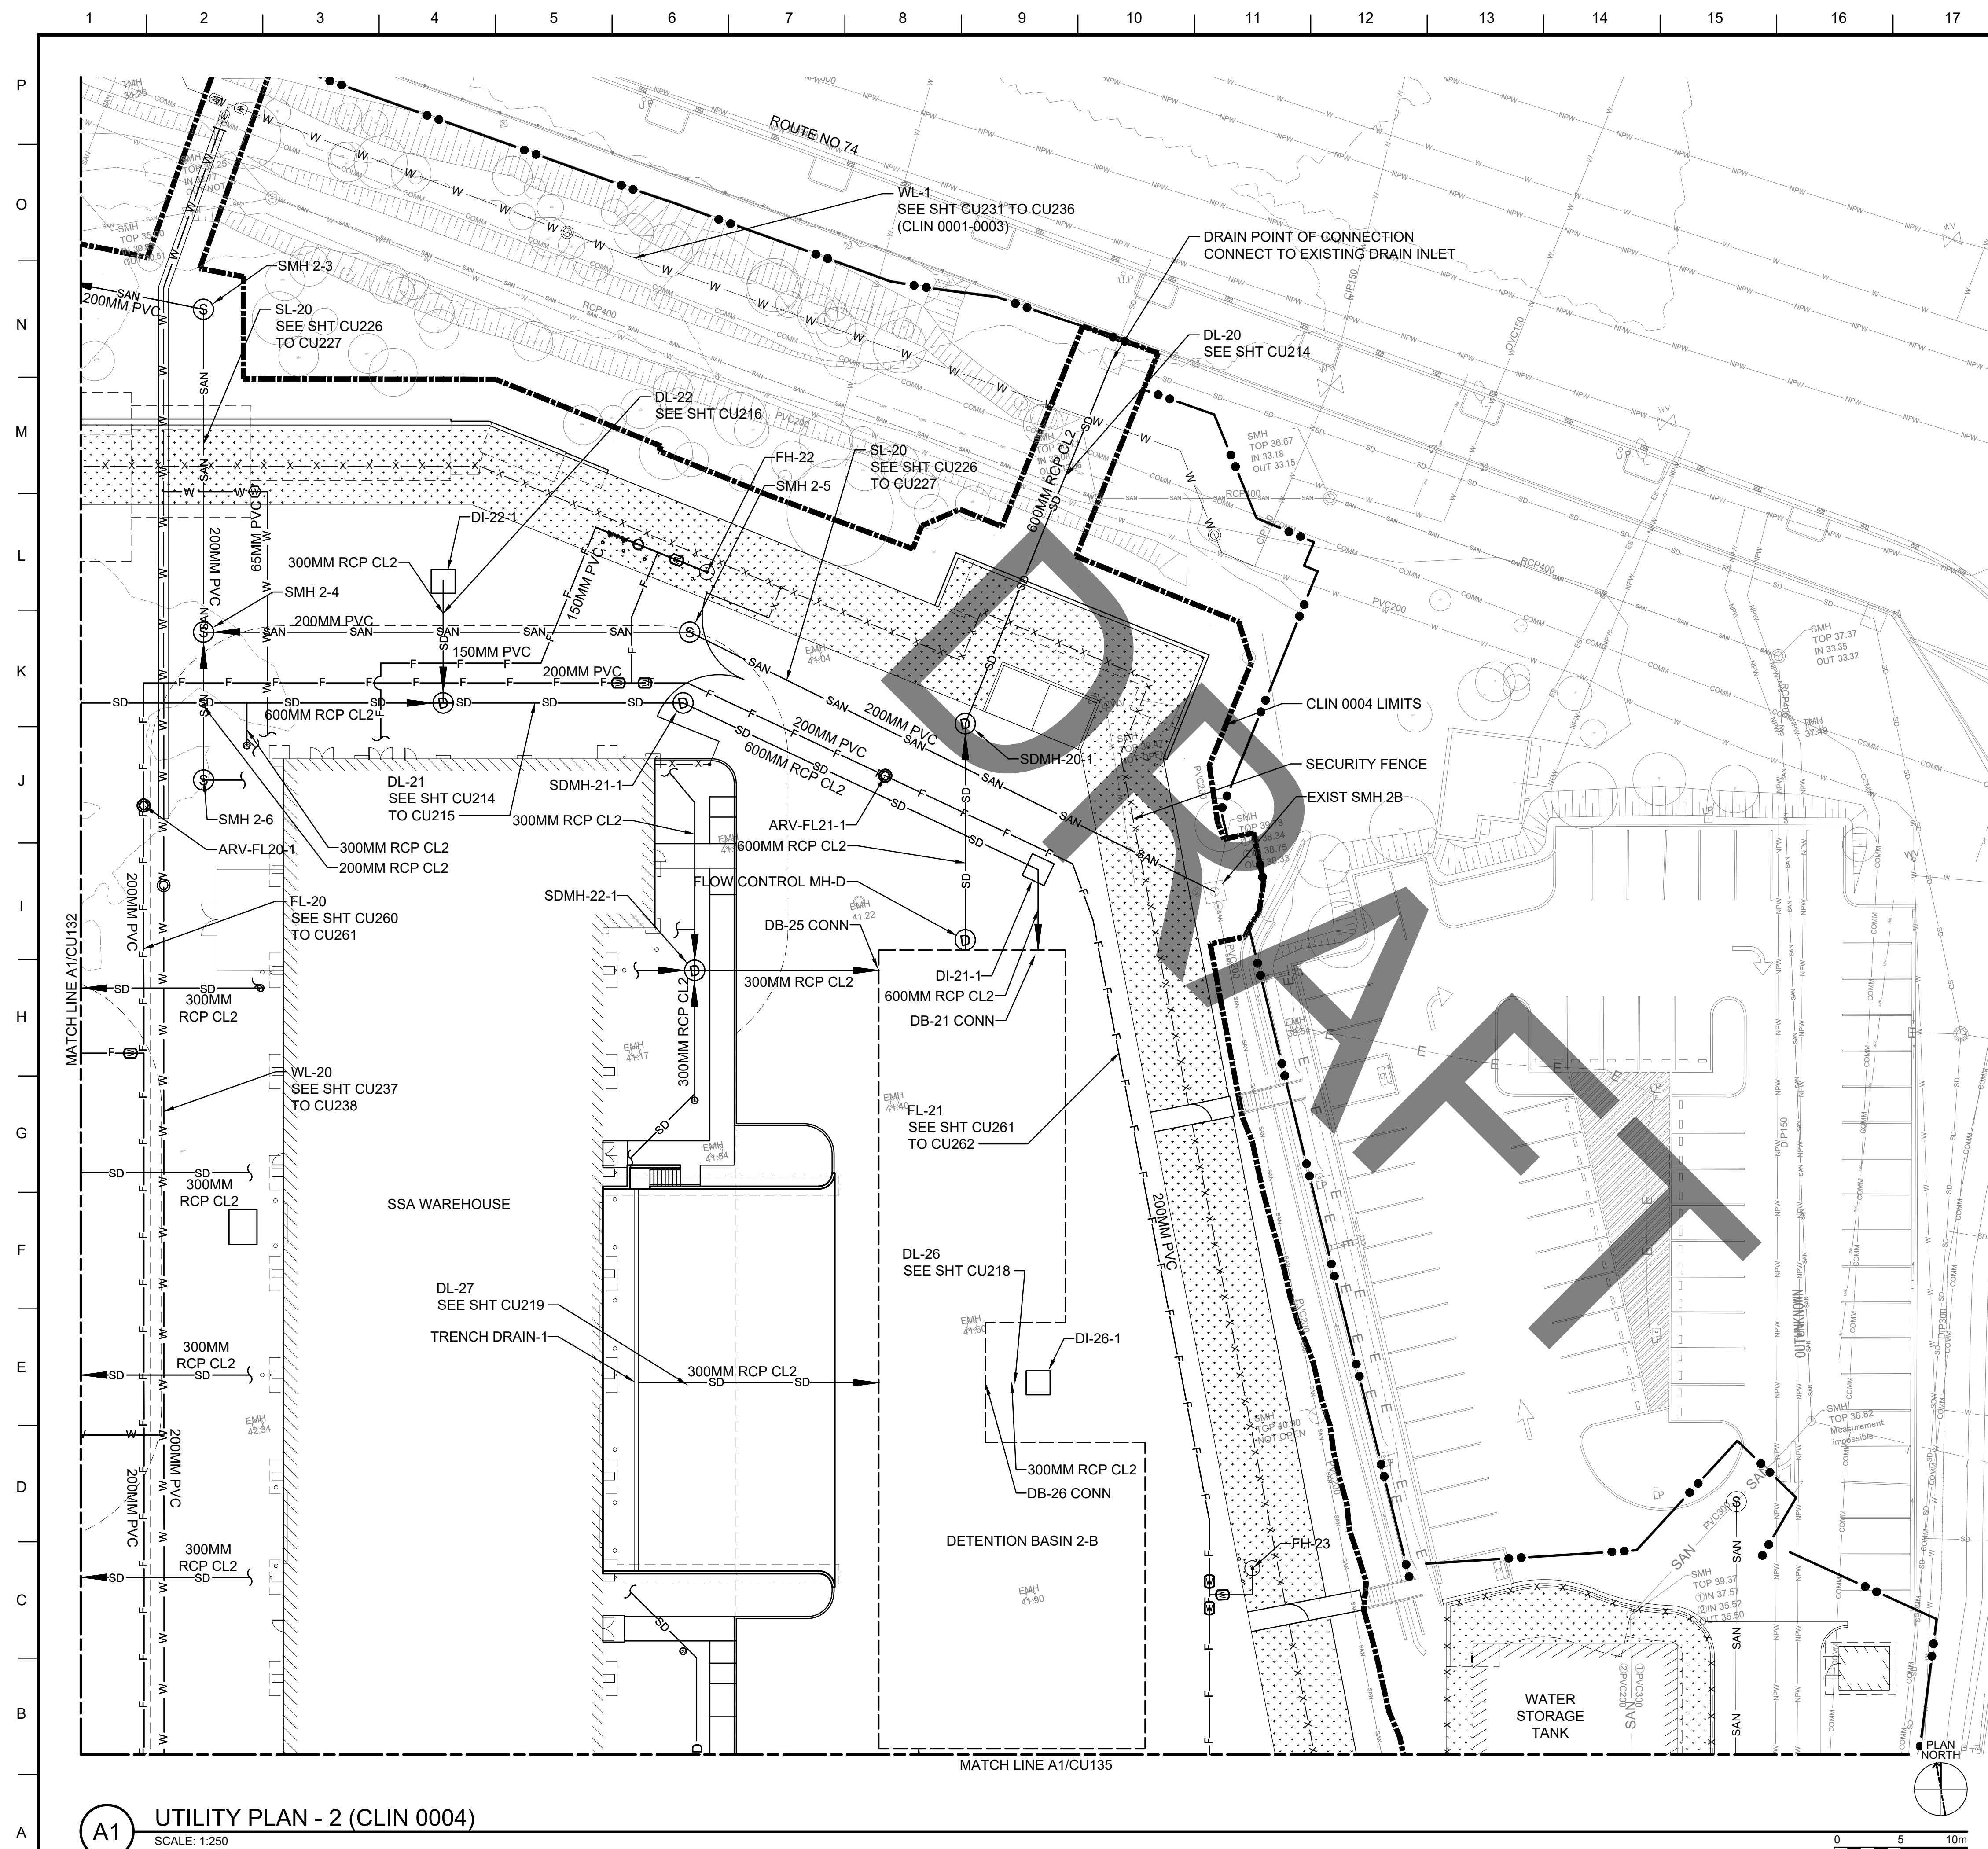


GENERAL NOTES

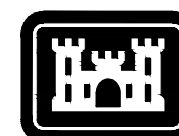

**US Army Corps
of Engineers®**

[illegible]

 US ARMY CORPS OF ENGINEERS JAPAN DISTRICT AREA OFFICE ISAFD, UNIT 34132 APO, AP 96374-5132	DESIGNED BY: DRAWN BY: CHECKED BY: SUBMITTED BY:	ISSUE DATE: SOLICITATION NO.: CONTRACT NO.: SCALE: AS SHOWN
 SSM INTERNATIONAL, INC 501 HONOLULU AVENUE, SUITE # 620 HONOLULU, HAWAII 96813	DATE: SCA 1	FILE NAME:


KADENA AIR BASE, OKINAWA, JAPAN
VEHICLE MAINTENANCE SHOP
FY20 MCA PN77833

UTILITY PLAN - 2 (CLIN 0004)


SHEET ID

CU133

SHEET LEGEND

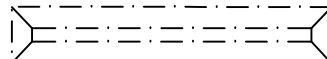
	PROJECT LIMITS
	SWALE
	DRAINLINE
	SEWERLINE
	WATERLINE
	FIRELINE
	DRAIN MANHOLE
	SEWER MANHOLE
	FIRE HYDRANT
	CLIN 0004: TEMPORARY FACILITIES (COF SS) DEMOLITION OF 8 EXISTING BUILDINGS SITE PREPARATION, FENCING, AND CLEARING OF SSA SUPPLY SUPPORT ACTIVITY (SSA) WAREHOUSE STORAGE SHED FOR SSA PARKING AND PAVING FOR SSA

KEY PLAN

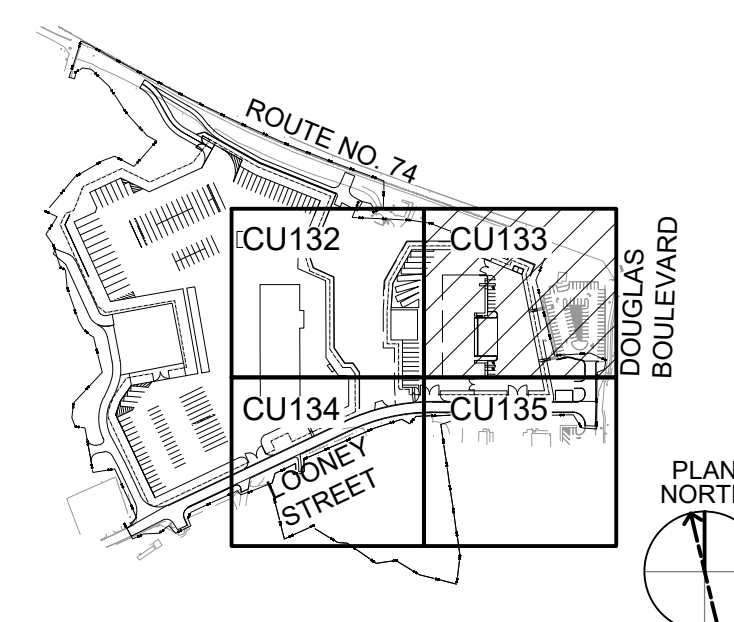


PLAN NORTH

INTERMEDIATE DESIGN

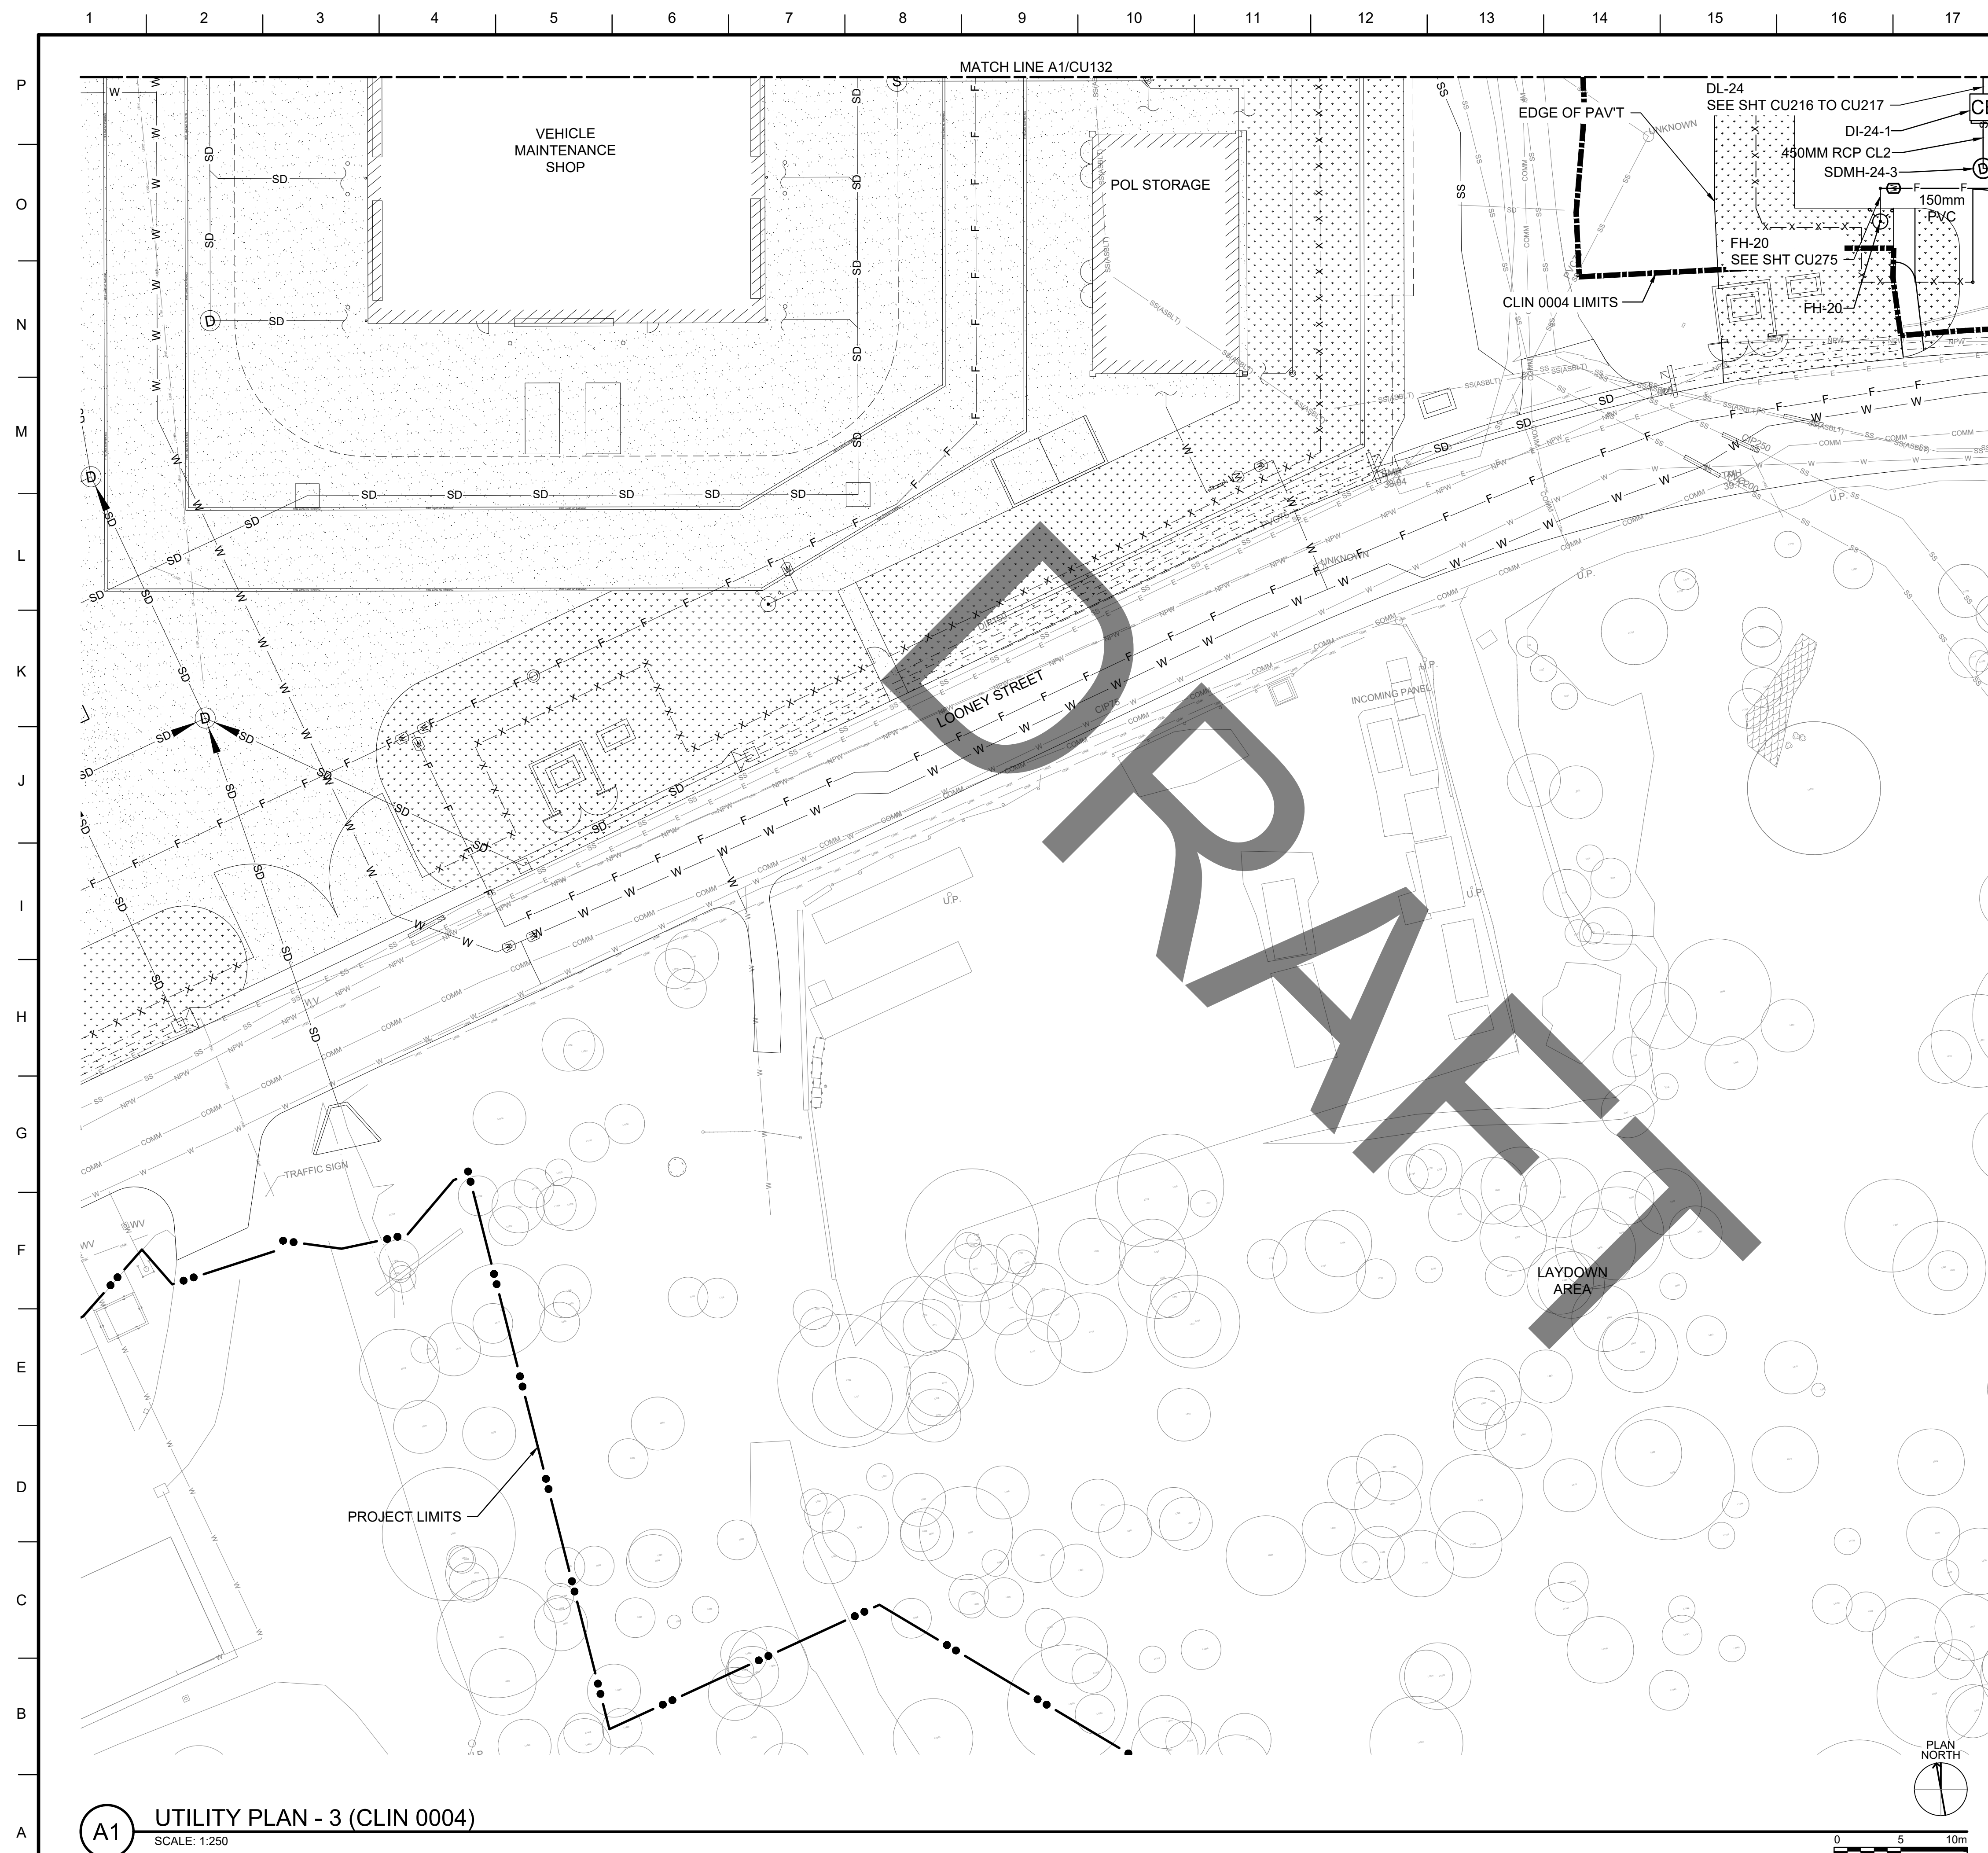

GENERAL NOTES

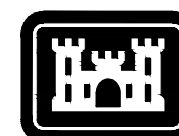

**US Army Corps
of Engineers®**

[illegible]

US ARMY CORPS OF ENGINEERS JAPAN DISTRICT, OKINAWA AREA OFFICE USAED-J, UNIT 35132 APO, AP 96374-5132	DESIGNED BY:	ISSUE DATE:
	DRAWN BY:	SOLICITATION NO.:
	CHECKED BY:	CONTRACT NO.:
	SUBMITTED BY:	SCALE:
	SIZE:	FILE NAME:


KADENA AIR BASE, OKINAWA, JAPAN
VEHICLE MAINTENANCE SHOP
FY20 MCA PN77833

UTILITY PLAN - 3 (CLIN 0004)


SHEET ID

CU134

SHEET LEGEND

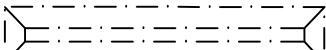
	PROJECT LIMITS
	SWALE
	DRAINLINE
	SEWERLINE
	WATERLINE
	FIRELINE
	DRAIN MANHOLE
	SEWER MANHOLE
	FIRE HYDRANT
	CLIN 0004: TEMPORARY FACILITIES (COF SS) DEMOLITION OF 8 EXISTING BUILDINGS SITE PREPARATION, FENCING, AND CLEARING OF SSA SUPPLY SUPPORT ACTIVITY (SSA) WAREHOUSE STORAGE SHED FOR SSA PARKING AND PAVING FOR SSA

KEY PLAN

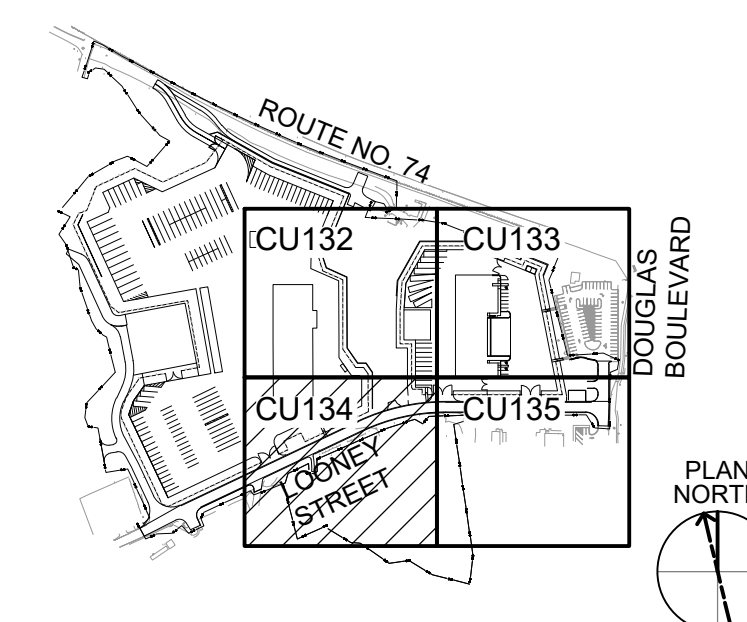

CLIN 0004

INTERMEDIATE DESIGN

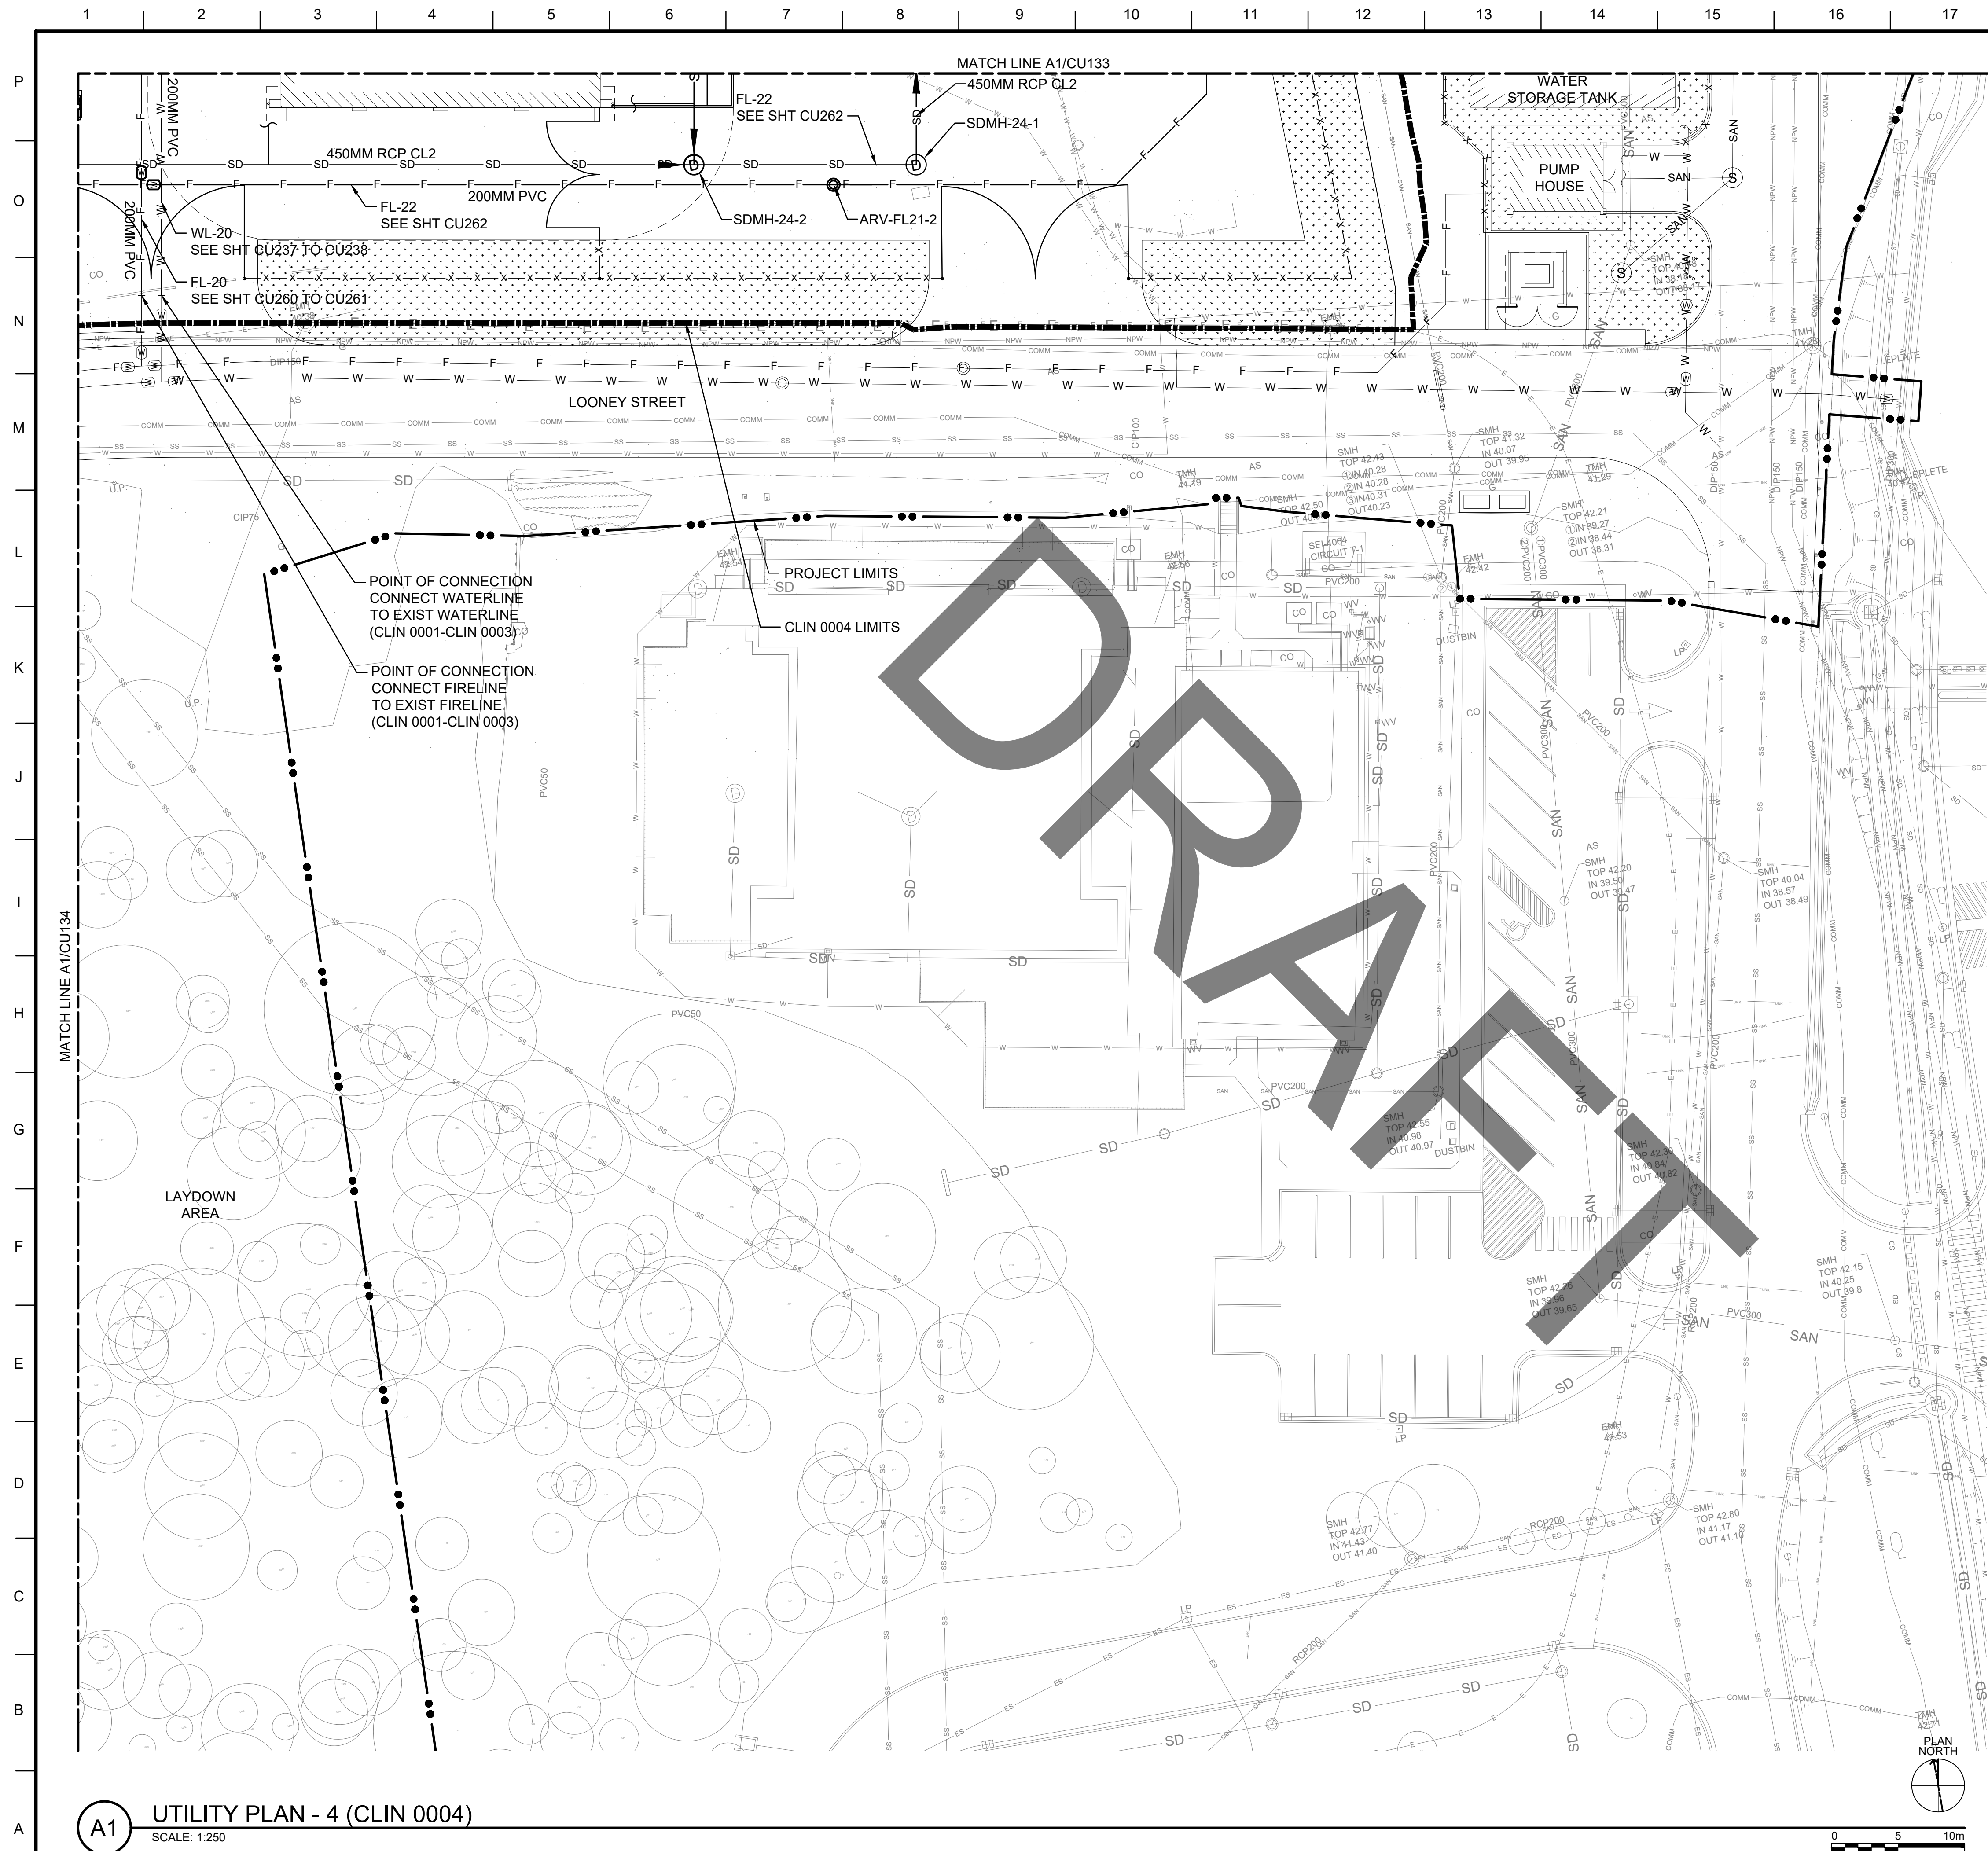


GENERAL NOTES

SHEET LEGEND

- PROJECT LIMITS
- SWALE
- SD DRAINLINE
- SAN SEWERLINE
- W WATERLINE
- F FIRELINE
- ⊙ DRAIN MANHOLE
- ⊙ SEWER MANHOLE
- ⊙ FIRE HYDRANT
- CLIN 0004:
TEMPORARY FACILITIES (COF SS)
DEMOLITION OF 8 EXISTING BUILDINGS
SITE PREPARATION, FENCING, AND
CLEARING OF SSA
SUPPLY SUPPORT ACTIVITY (SSA)
WAREHOUSE STORAGE SHED FOR SSA
PARKING AND PAVING FOR SSA

CLIN 0004

KEY PLAN

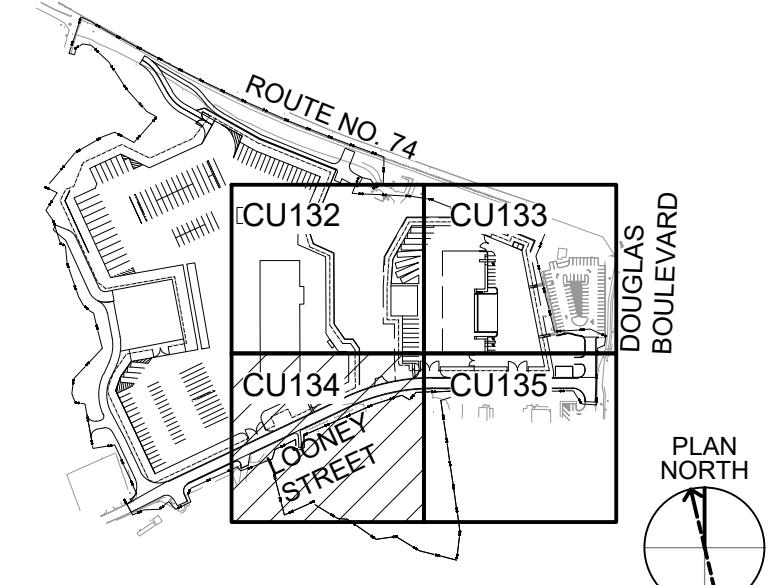

US Army Corps of Engineers

ISSUE DATE:	
DESIGNED BY:	SOLICITATION NO.:
DRAWN BY:	CONTRACT NO.:
CHECKED BY:	SCALE:
SUBMITTED BY:	AS SHOWN
SIZE:	FILE NAME:
ISO A1	

US ARMY CORPS OF ENGINEERS
JAPAN DISTRICT, OKINAWA AREA OFFICE
USAFED-J UNIT 55132
APO AP 96374-5132

SSEM
SSEM INTERNATIONAL, INC.
501 SUMNER STREET, SUITE 620
HONOLULU, HAWAII 96817


KADENA AIR BASE, OKINAWA, JAPAN
VEHICLE MAINTENANCE SHOP
FY20 MCA PN77833


UTILITY PLAN - 4 (CLIN 0004)

SHEET ID

CU135

INTERMEDIATE DESIGN

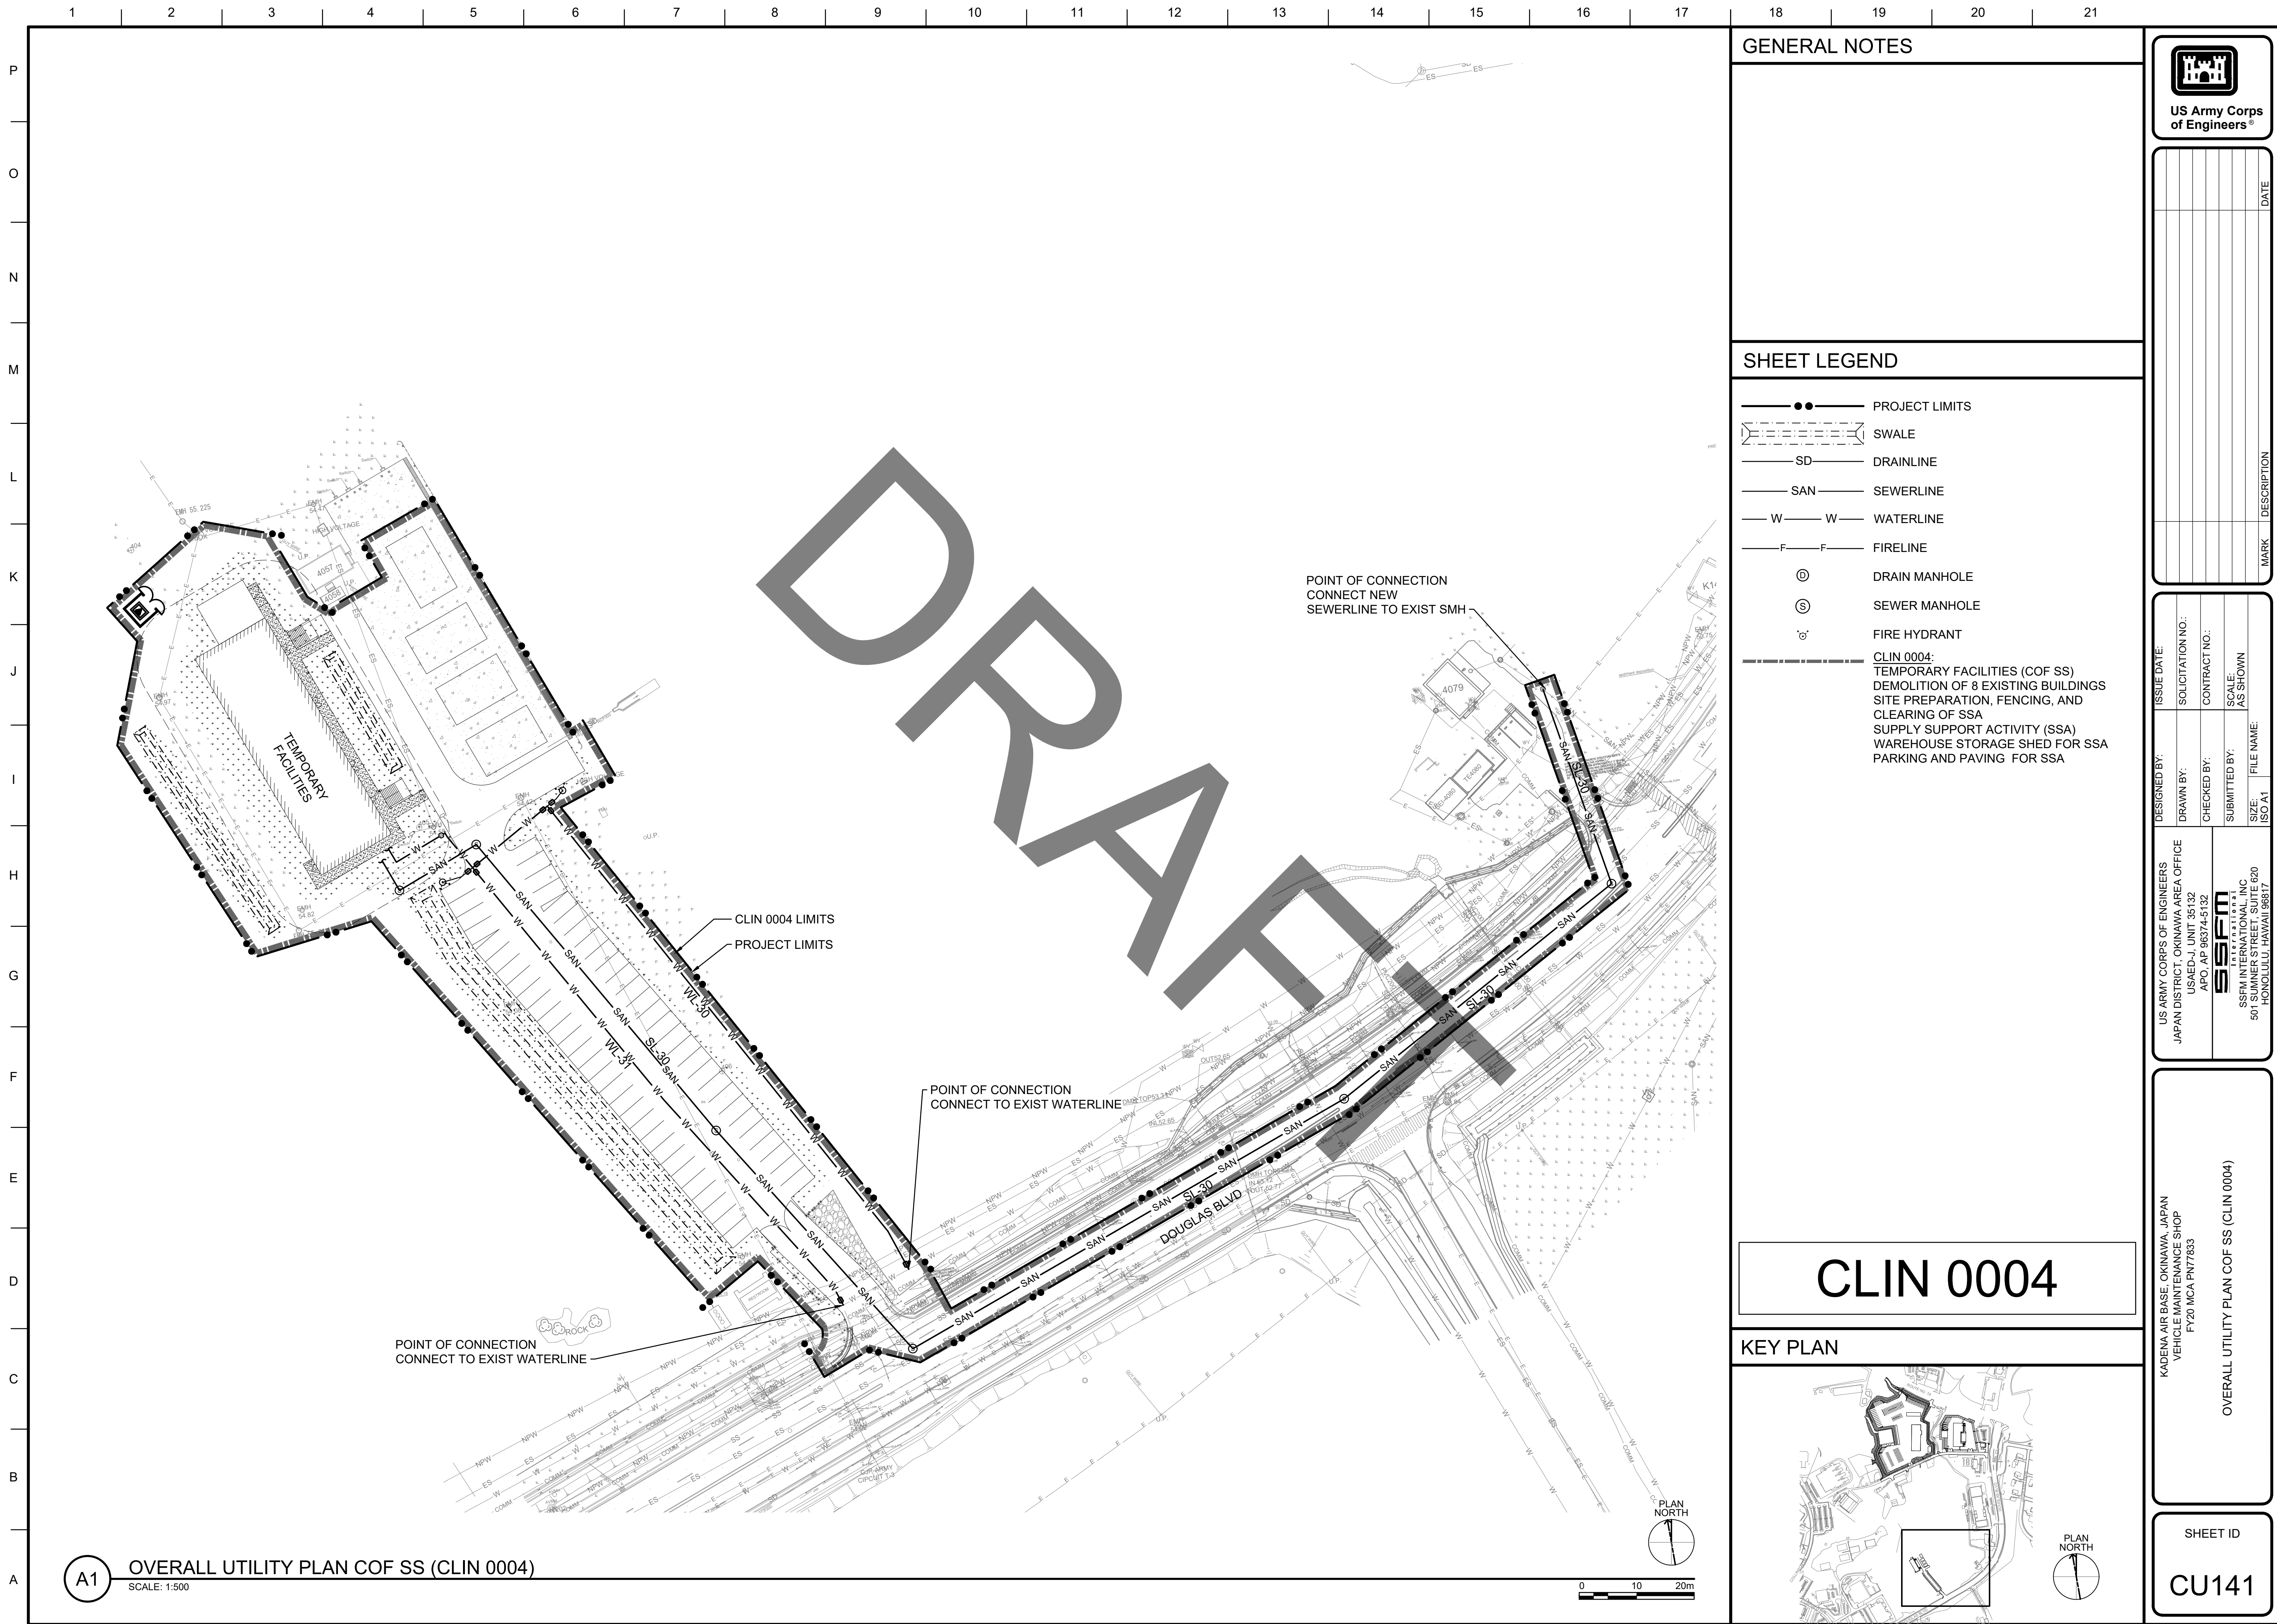

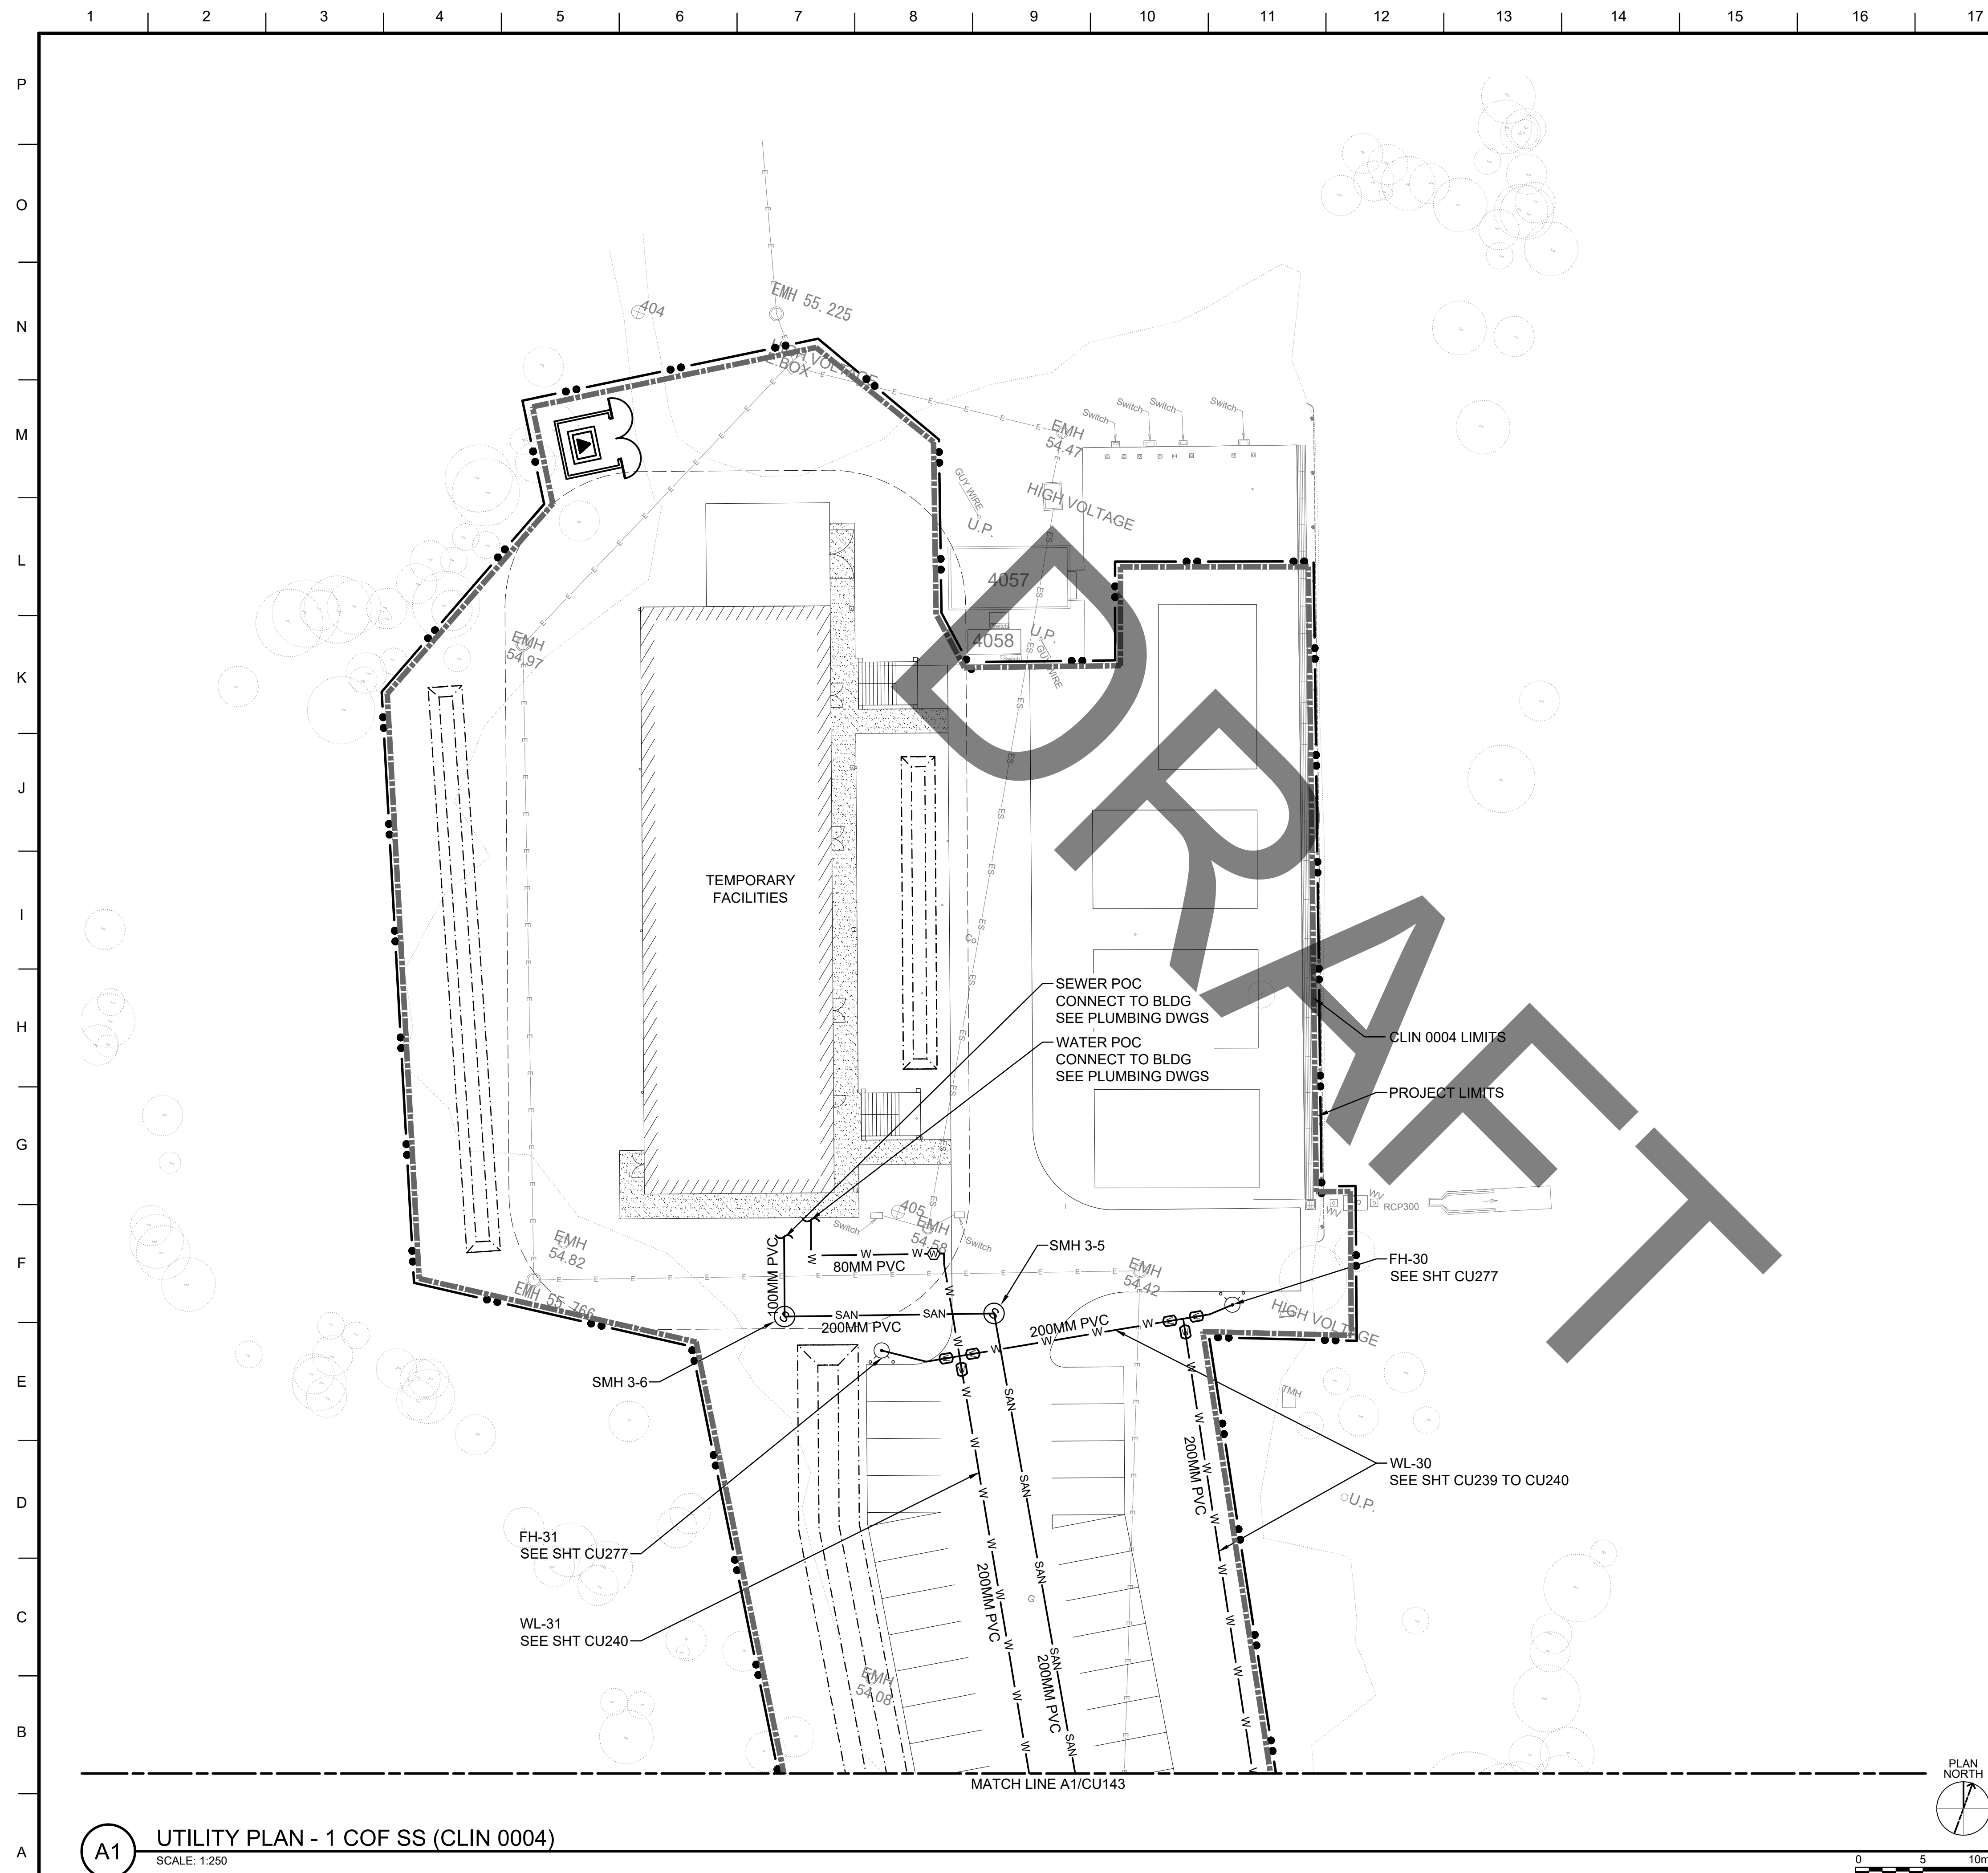

GENERAL NOTES



US Army Corps
of Engineers®


[illegible]

SHEET LEGEND

	PROJECT LIMITS
	SWALE
	DRAINLINE
	SEWERLINE
	WATERLINE
	FIRELINE
	DRAIN MANHOLE
	SEWER MANHOLE
	FIRE HYDRANT
	CLIN 0004: TEMPORARY FACILITIES (COF SS) DEMOLITION OF 8 EXISTING BUILDINGS SITE PREPARATION, FENCING, AND CLEARING OF SSA SUPPLY SUPPORT ACTIVITY (SSA) WAREHOUSE STORAGE SHED FOR SSA PARKING AND PAVING FOR SSA

JAPAN DISTRICT, OKINAWA AREA OFFICE USAED-4, UNIT 35132 APO, AP 96374-5132	DRAWN BY:	SOLICITATION NO.:
	CHECKED BY:	CONTRACT NO.:
	SUBMITTED BY:	SCALE: AS SHOWN
	SIZE:	FILE NAME: ISO A1

KEY PLAN

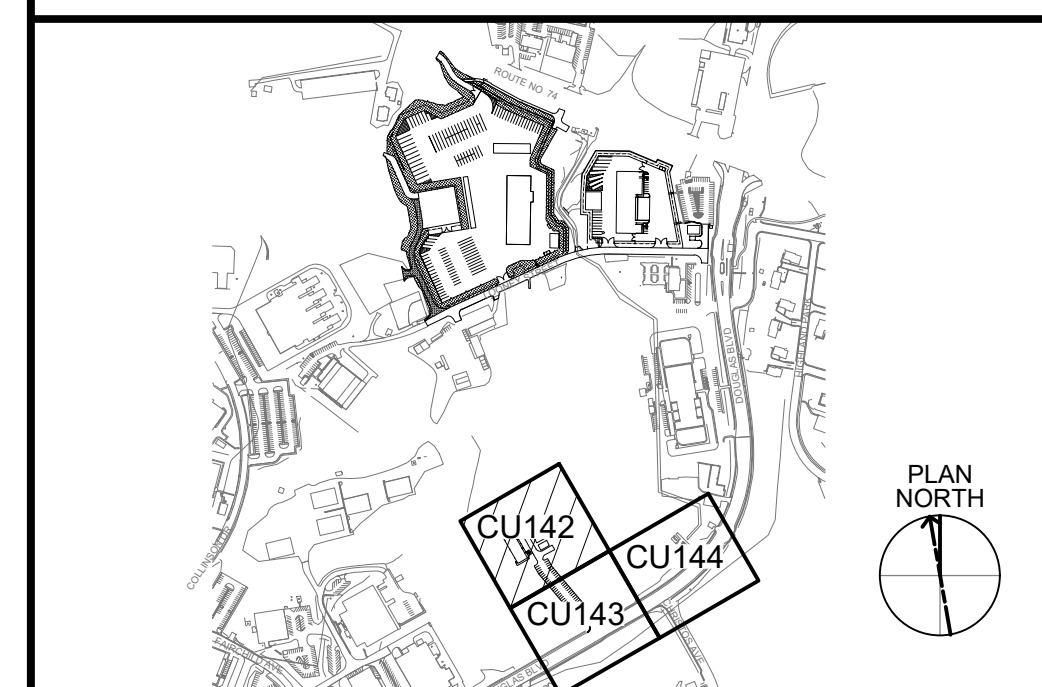


VEHICLE MAINTENANCE SHOP
FY20 MCA PN77833

SHEET ID

CU142

INTERMEDIATE DESIGN

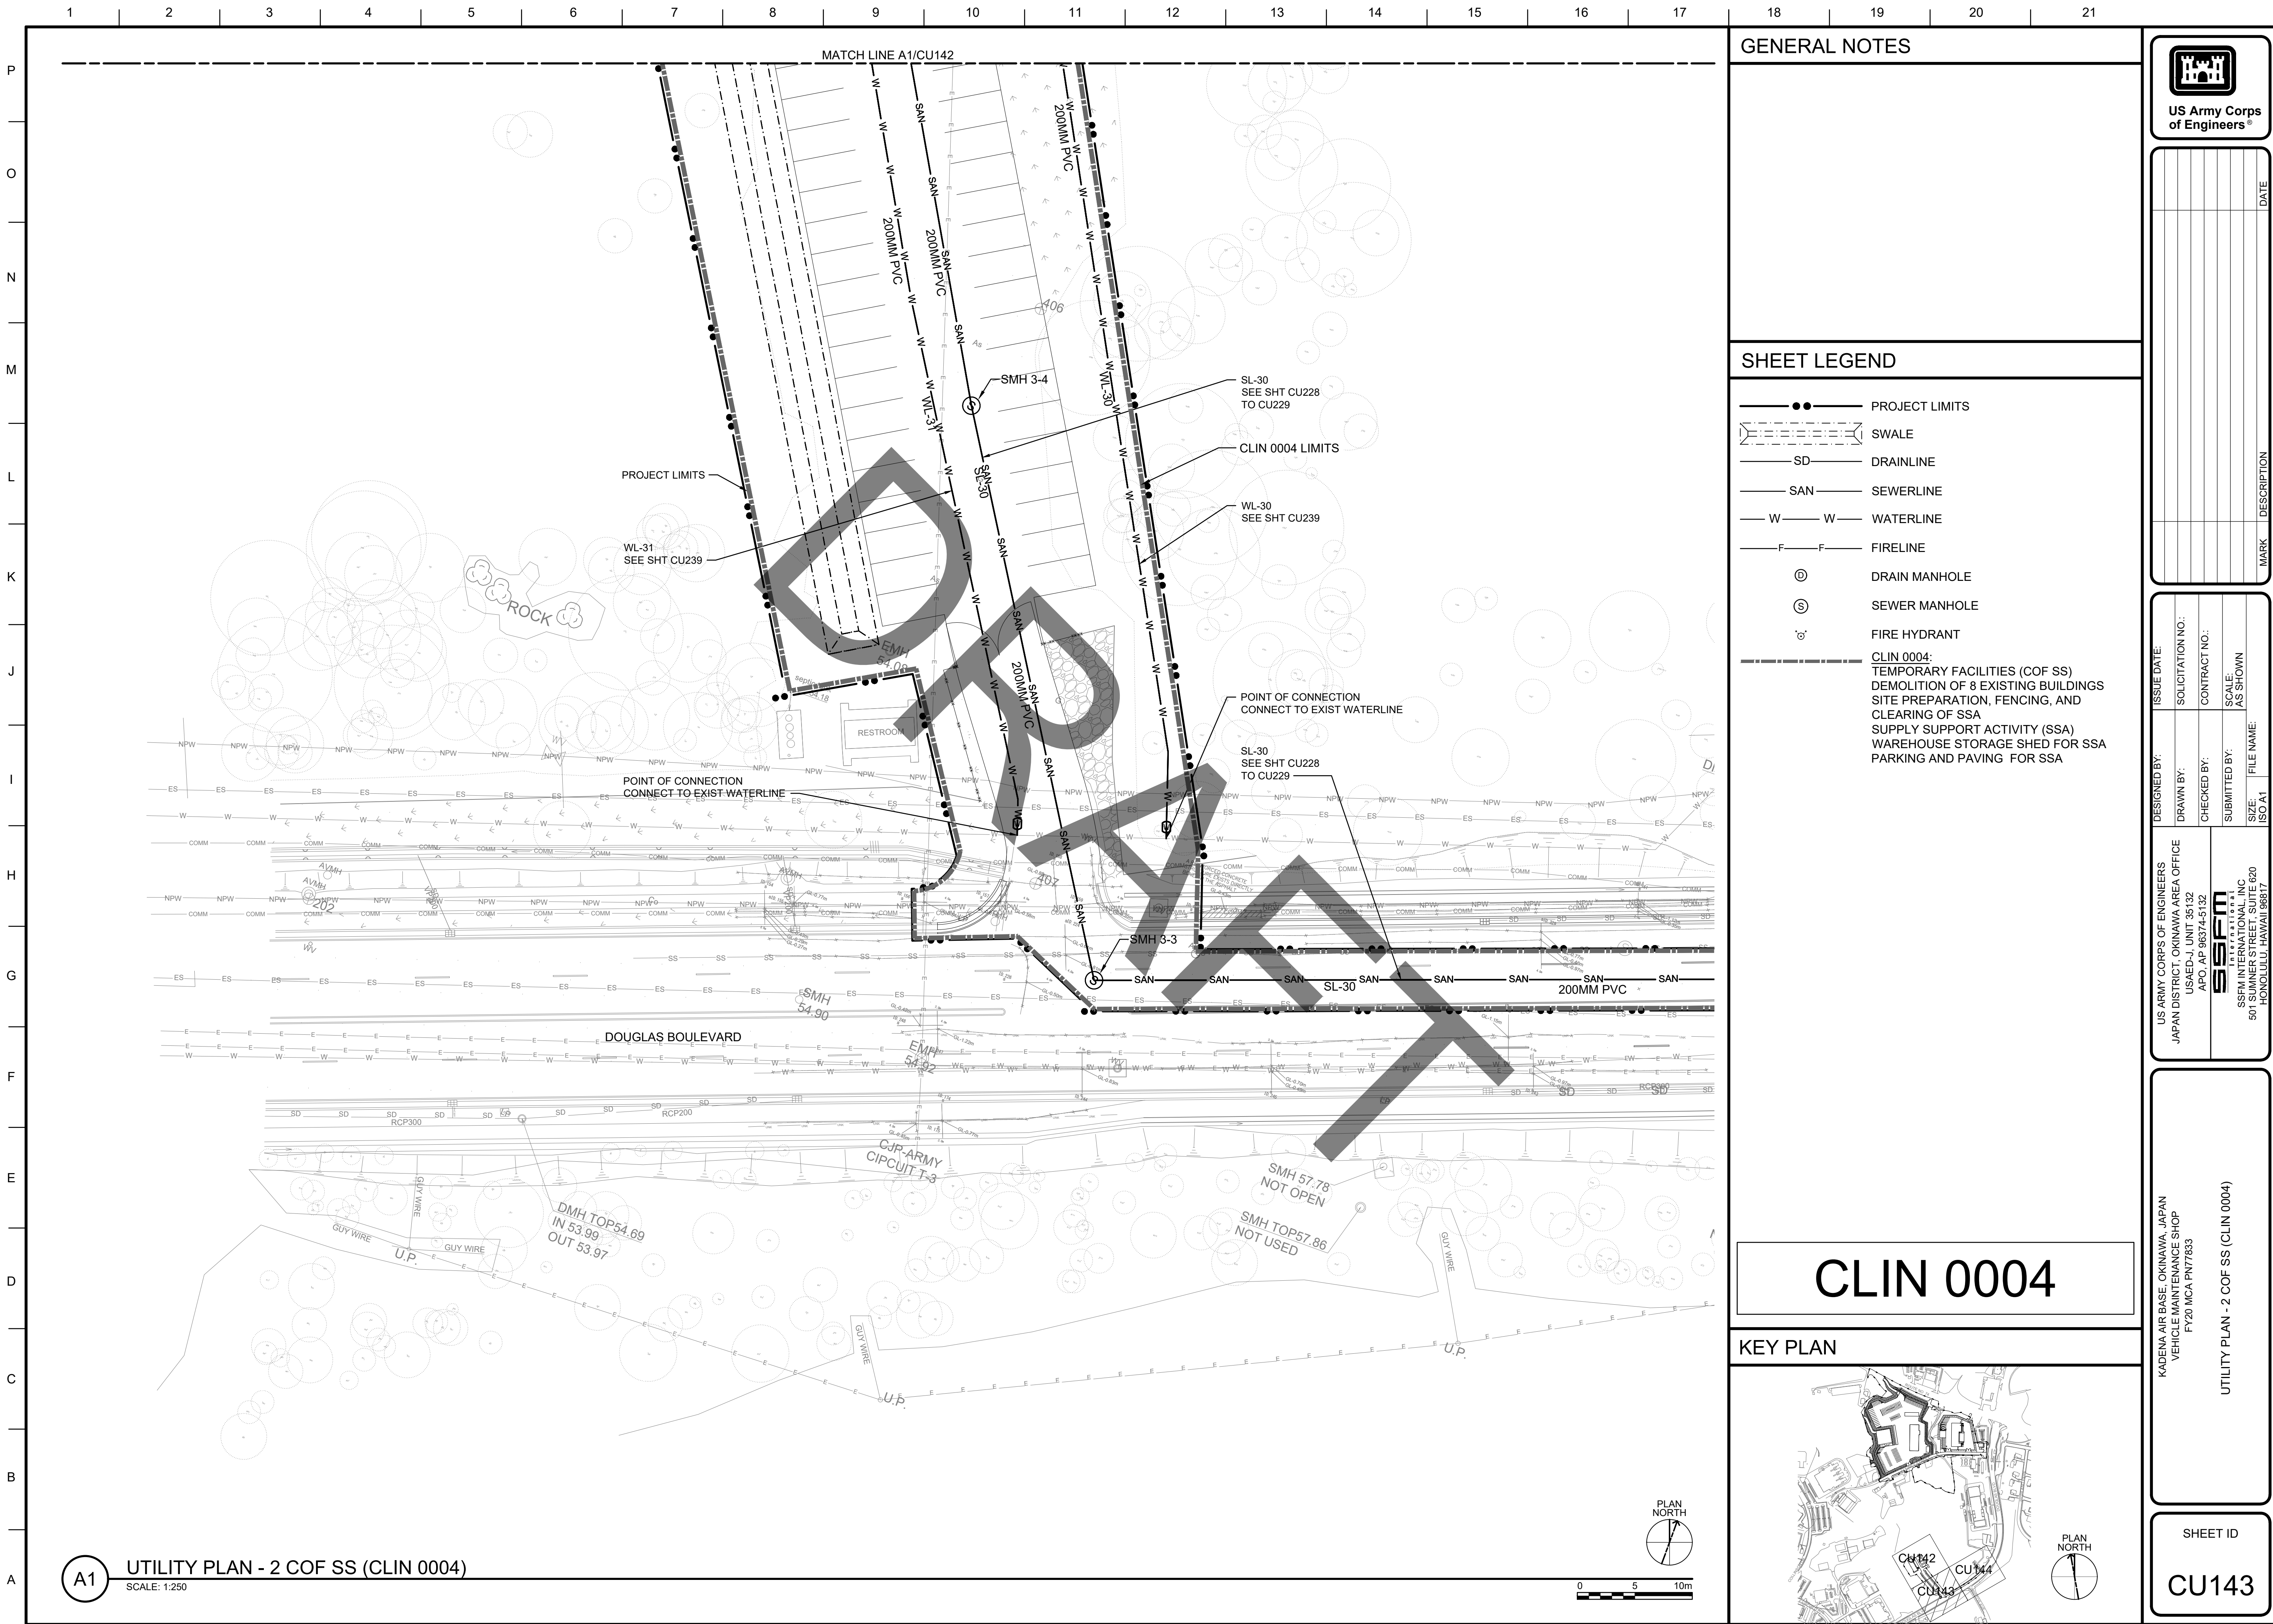


GENERAL NOTES

SHEET LEGEND

- PROJECT LIMITS
- SWALE
- DRAINLINE
- SEWERLINE
- WATERLINE
- FIRELINE
- DRAIN MANHOLE
- SEWER MANHOLE
- FIRE HYDRANT
- CLIN 0004:
TEMPORARY FACILITIES (COF SS)
DEMOLITION OF 8 EXISTING BUILDINGS
SITE PREPARATION, FENCING, AND
CLEARING OF SSA
SUPPLY SUPPORT ACTIVITY (SSA)
WAREHOUSE STORAGE SHED FOR SSA
PARKING AND PAVING FOR SSA

CLIN 0004

KEY PLAN

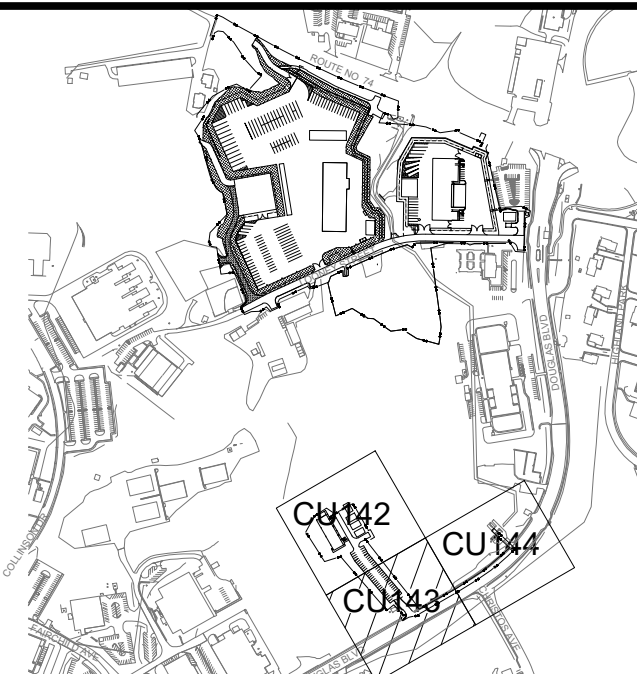

US Army Corps of Engineers

ISSUE DATE:	
DESIGNED BY:	SOLICITATION NO.:
DRAWN BY:	CONTRACT NO.:
CHECKED BY:	SCALE:
SUBMITTED BY:	AS SHOWN
SIZE:	FILE NAME:
ISO A1	

US ARMY CORPS OF ENGINEERS
JAPAN DISTRICT, OKINAWA AREA OFFICE
USAFED-J UNIT 35132
APO, AP 96374-5132

SSFM
SSFM INTERNATIONAL, INC.
501 SUMNER STREET, SUITE 620
HONOLULU, HAWAII 96817


KADENA AIR BASE, OKINAWA, JAPAN
VEHICLE MAINTENANCE SHOP
FY20 MCA PN77833

UTILITY PLAN - 2 COF SS (CLIN 0004)

SHEET ID

CU143

INTERMEDIATE DESIGN

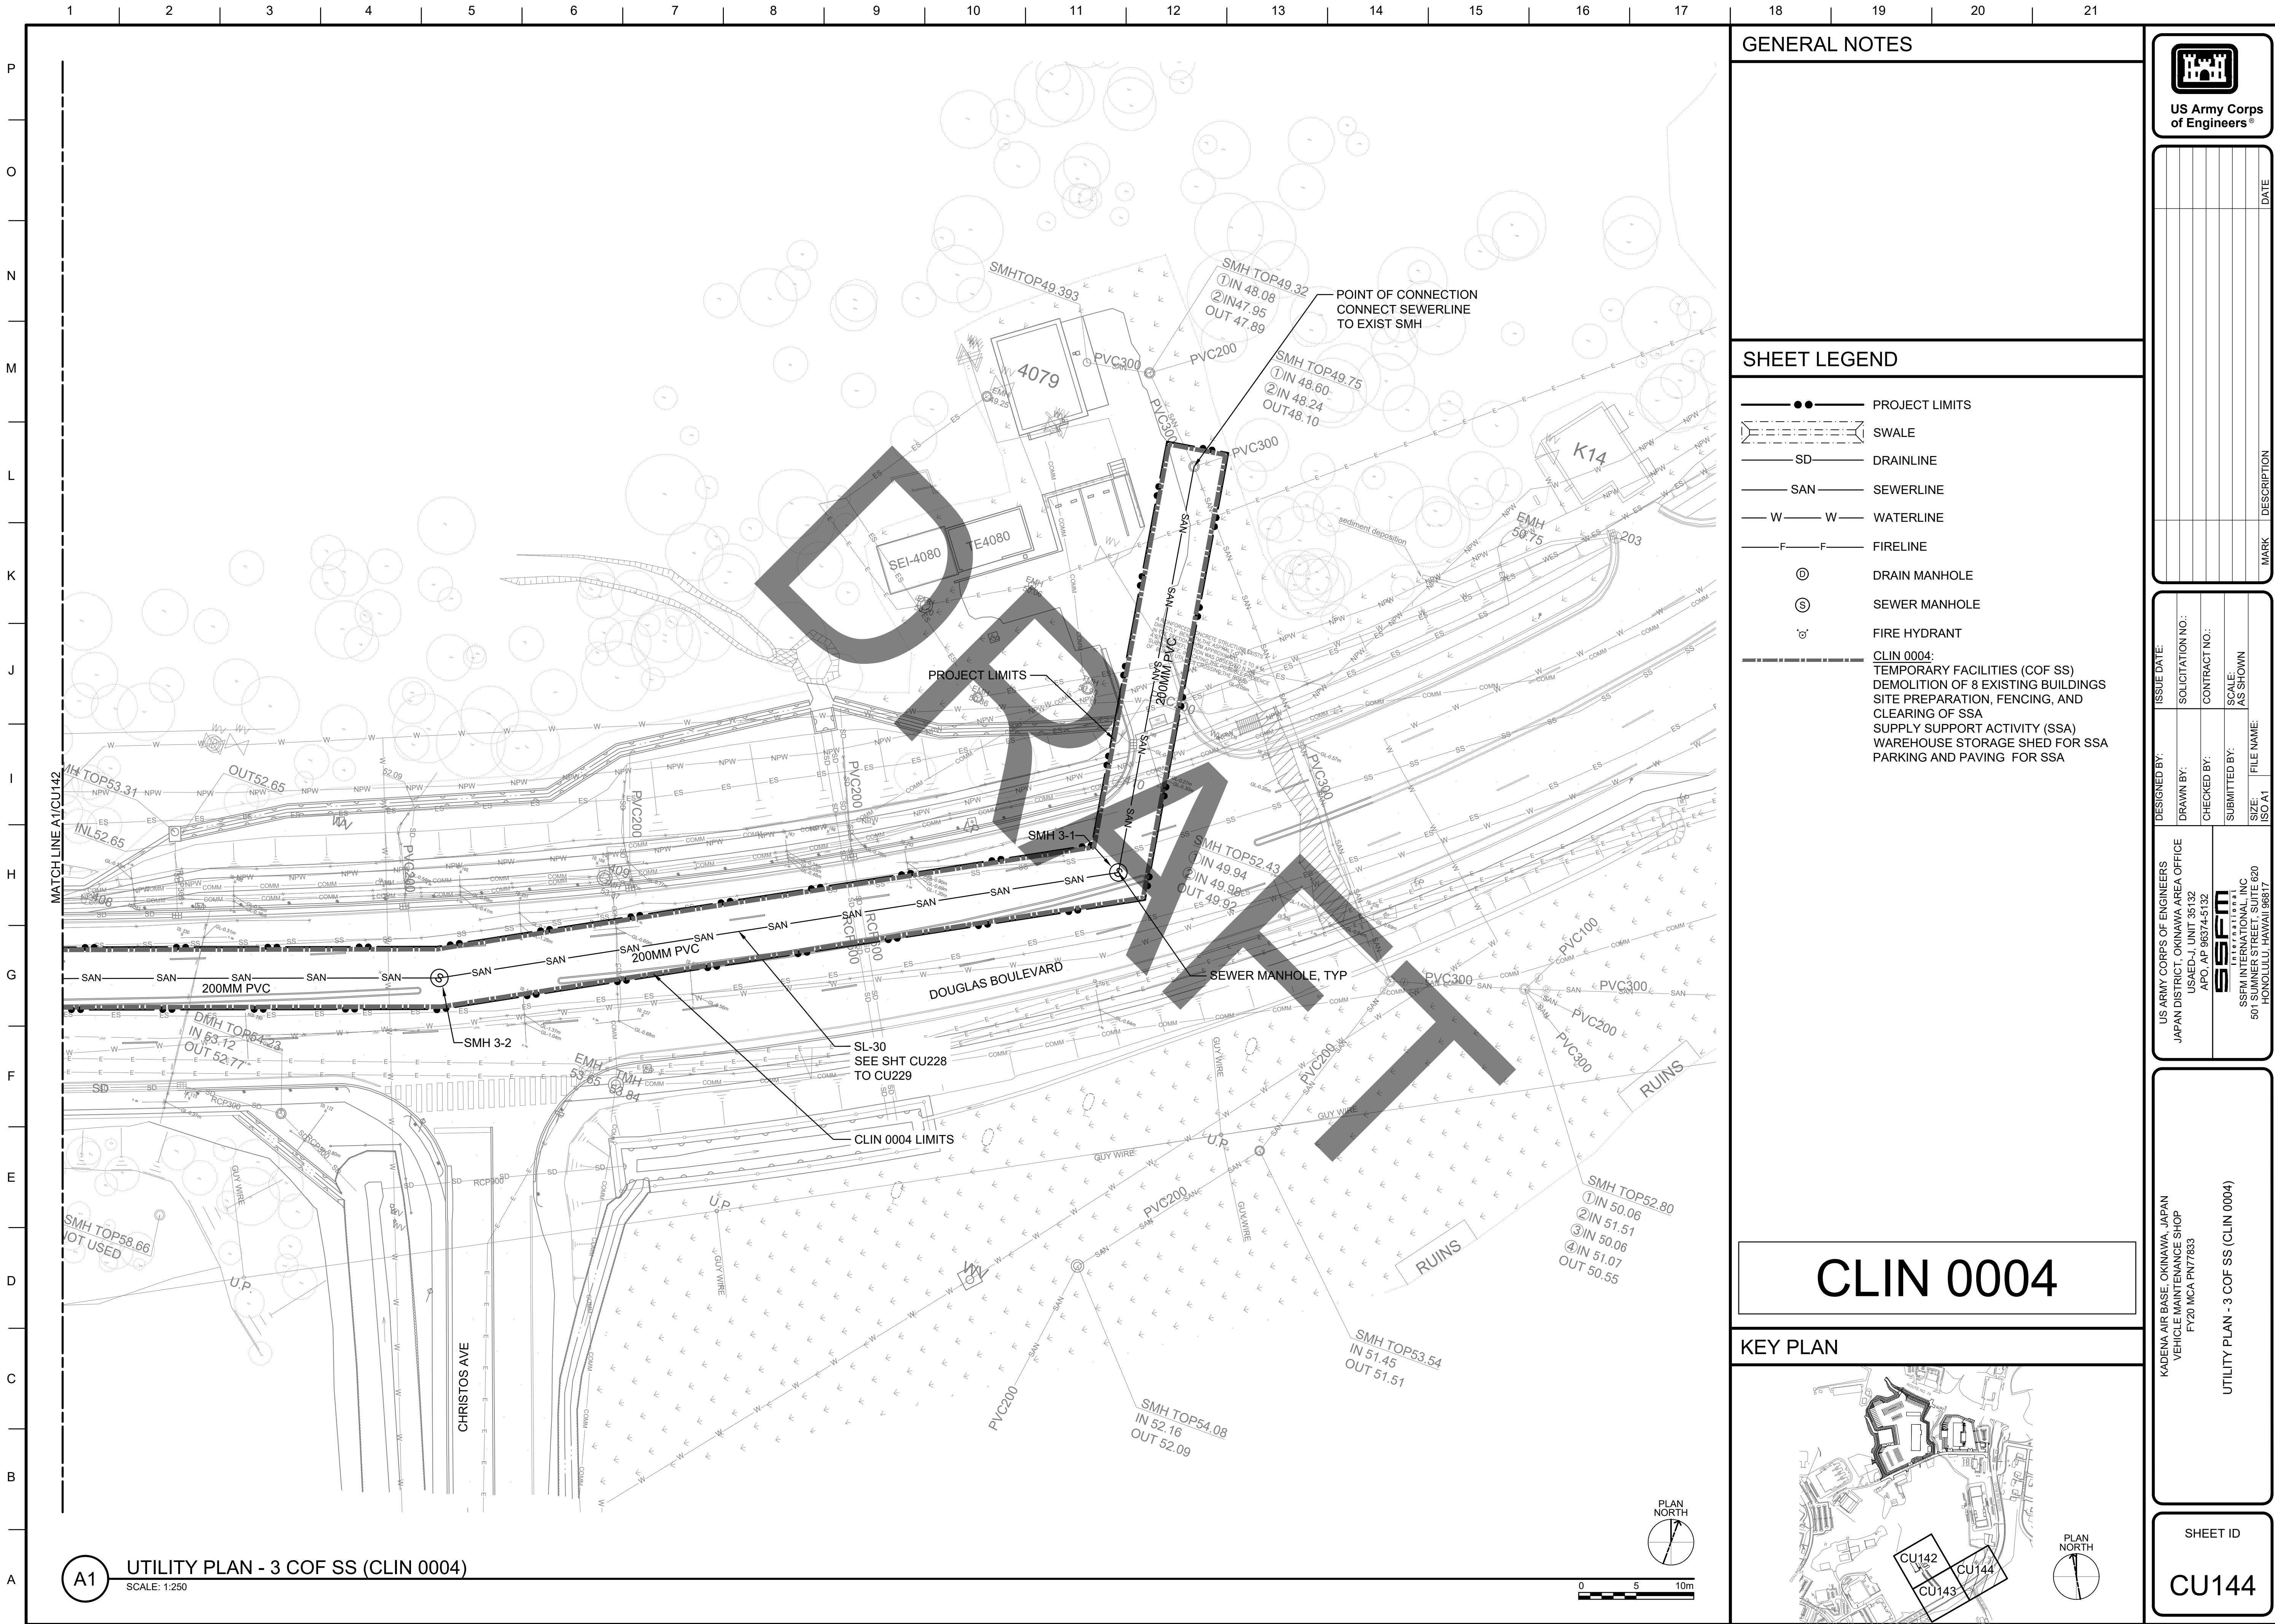


GENERAL NOTES

SHEET LEGEND

- PROJECT LIMITS
- SWALE
- DRAINLINE
- SEWERLINE
- WATERLINE
- FIRELINE
- DRAIN MANHOLE
- SEWER MANHOLE
- FIRE HYDRANT
- CLIN 0004:
TEMPORARY FACILITIES (COF SS)
DEMOLITION OF 8 EXISTING BUILDINGS
SITE PREPARATION, FENCING, AND
CLEARING OF SSA
SUPPLY SUPPORT ACTIVITY (SSA)
WAREHOUSE STORAGE SHED FOR SSA
PARKING AND PAVING FOR SSA

CLIN 0004

KEY PLAN

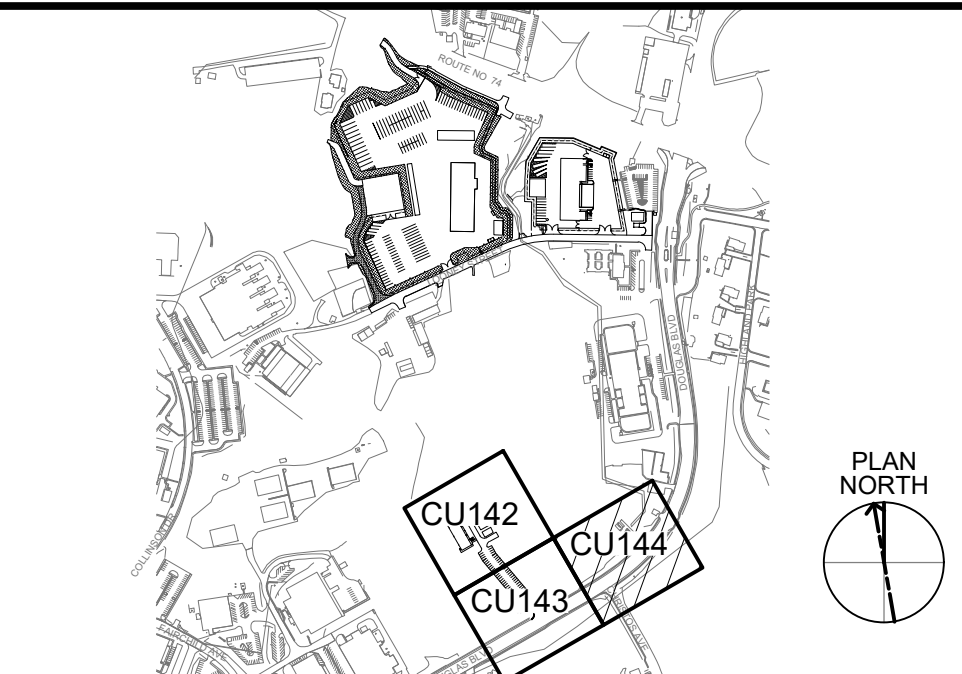

US Army Corps of Engineers®

ISSUE DATE:		SOLICITATION NO.:		CONTRACT NO.:	
DESIGNED BY:	DRAWN BY:	CHECKED BY:	SUBMITTED BY:	SCALE:	AS SHOWN
US ARMY CORPS OF ENGINEERS JAPAN DISTRICT, OKINAWA AREA OFFICE USAD-J, UNIT 35132 APO, AP 96374-5132		SSM INTERNATIONAL, INC. 501 SUMNER STREET, SUITE 620 HONOLULU, HAWAII 96817			

KADENA AIR BASE, OKINAWA, JAPAN
VEHICLE MAINTENANCE SHOP
FY20 MCA PN77833

UTILITY PLAN - 3 COF SS (CLIN 0004)

SHEET ID

CU144

INTERMEDIATE DESIGN

