



U.S. Department of Veterans Affairs
Veterans Health Administration


RENOVATE BUILDING 1

GULF COAST VETERANS HEALTH CARE SYSTEM

BILOXI, MISSISSIPPI

PROJECT NO. 520-317X
CONTRACT NO. VA101F-17-D-2902
36C10F18R0660


OWNER	RESIDENT ENGINEER	ARCHITECT	STRUCTURAL ENGINEER	MECHANICAL ENGINEER	ELECTRICAL ENGINEER	TECHNOLOGY ENGINEER
VA HEALTH CARE CFM KHALED ZAATREH PROJECT MANAGER EMAIL: KHALED.ZAATREH@VA.GOV CONTACT NO: 682-377-5689 (D)	VA HEALTH CARE BILOXI XXXXXXX SENIOR RESIDENT ENGINEER EMAIL: CHRIS.LEVELLE@VA.GOV CONTACT NO: 228-523-5693 (D)	TOM OLESAK, ARCHITECT TOM OLESAK CONTACT NO: 952-451-0460	IMEG Corp. HEATHER HEIDENREICH CONTACT NO: 314-645-1132	IMEG Corp. PAUL EDWARD PARRY CONTACT NO: 314-645-1132	IMEG Corp. PAUL EDWARD PARRY CONTACT NO: 314-645-1132	IMEG Corp. PAUL EDWARD PARRY CONTACT NO: 314-645-1132

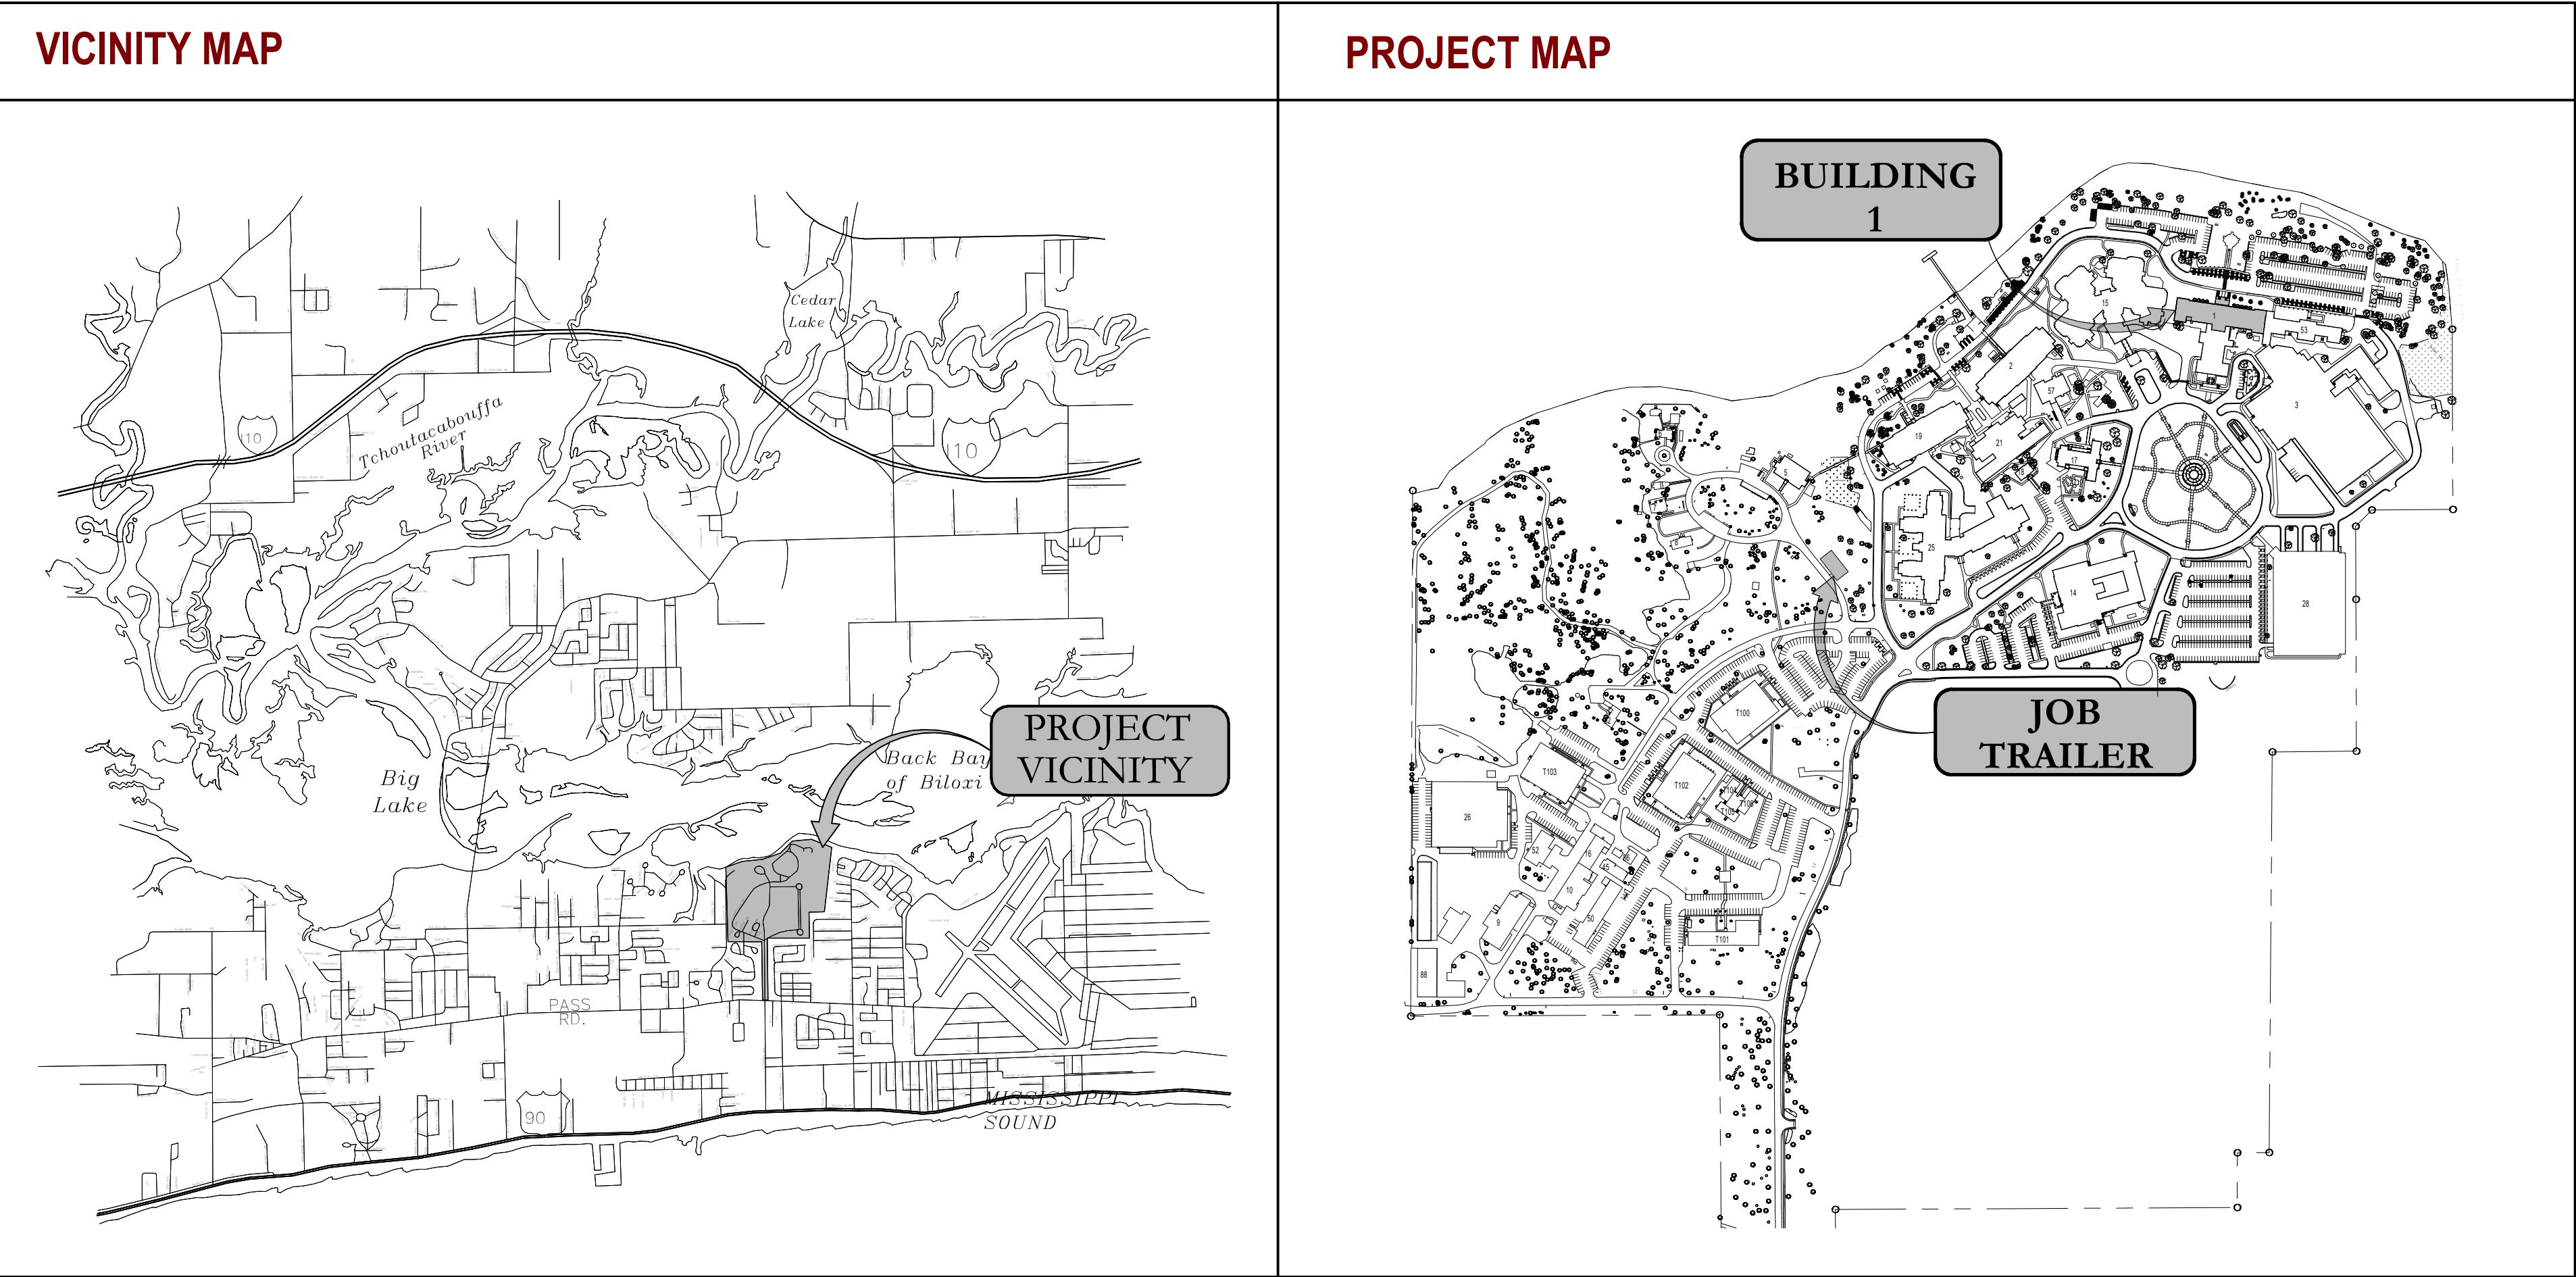

CONFORMED SET
FOR CONSTRUCTION

	</
--	--	----

C:\Users\pct\Documents\15090 - VAC-C-Biloxi Building 1_R25_Central.mxd_Yunyoung.nxd 5/14/2025 8:58:37 AM

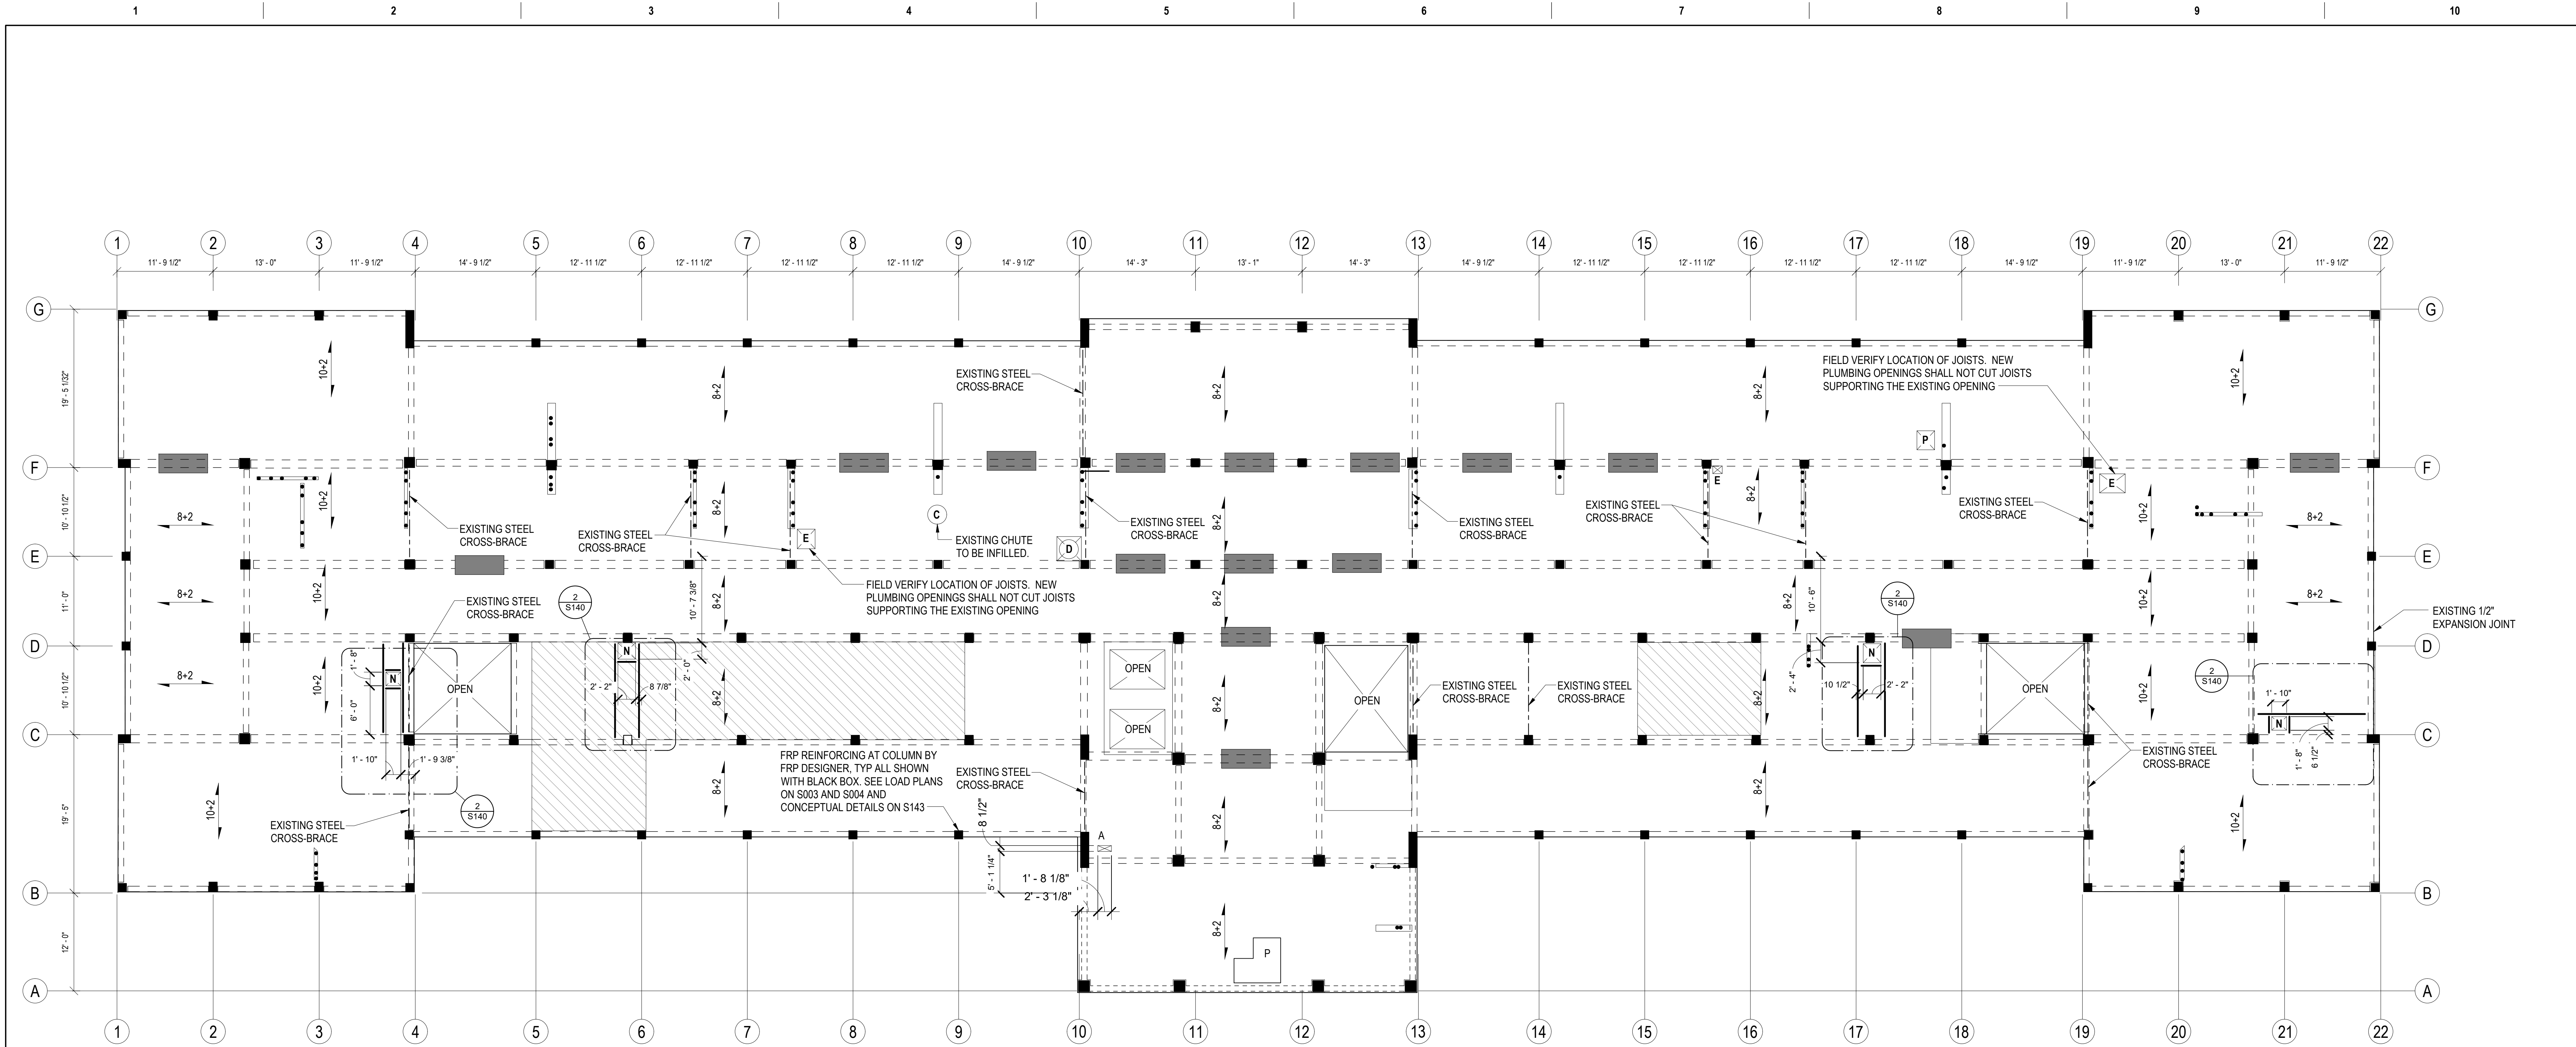

PLAN NORTH
1
FOURTH FLOOR FRAMING PLAN
1/8" = 1'-0"
FINISH FLOOR EL. 65'-6" (VIF)

LEGEND:


- [Solid Grey Box] = INDICATES FRP BEAM REPAIRS PREVIOUSLY COMPLETED.
- [Dashed Line with Dots] = PLUMBING CHASE THROUGH CONCRETE FLOOR, COORDINATE WITH MEP DRAWINGS. IF NEW CHASE IS PARALLEL TO CONCRETE JOIST SPANS, LOCATE OPENINGS TO AVOID CUTTING JOISTS.
IF NEW CHASE IS PERPENDICULAR TO CONCRETE JOIST SPANS, OR IF THE NEW OPENINGS OTHERWISE CUT THROUGH JOISTS, PROVIDE ADDITIONAL SUPPORT PER SHEET S140. REFER TO DETAILS 1, 2 OR 3 AS APPROPRIATE, DEPENDING ON HOW MANY ADJACENT JOISTS ARE CUT.
DO NOT CUT ANY PRIMARY BEAMS OR COLUMNS
- [8'-2" Joist Symbol] = EXISTING JOIST SPANS TYP. FLOOR 2" CONCRETE SLAB OVER 8" JOIST (8'-2") @ 25' O.C., TYP., U.N.O.
- [10'-2" Joist Symbol] = EXISTING JOIST SPANS TYP. FLOOR 2" CONCRETE SLAB OVER 10" JOIST (10'-2") @ 25' O.C., TYP., U.N.O.
- [Hatched Box] = AREAS OF DAMAGED CONCRETE, REFER TO S160.
- A = ACCESS HATCH.
- E = EXISTING EXHAUST TO REMAIN, FIELD VERIFY LOCATION AND SIZE.
- N = NEW EXHAUST, COORDINATE LOCATION WITH ARCH AND MEP DRAWINGS.
- C = EXISTING RUBBISH CHUTE TO BE INFILLED. REFER TO S160 FOR ADDITIONAL SLAB REPAIR INFORMATION.
- D = EXISTING RUBBISH CHUTE TO BE MODIFIED FOR NEW OPENING - REFER TO ARCHITECT FOR ADDITIONAL DETAILS.
- P = EXISTING PENETRATION THROUGH SLAB TO BE INFILLED. REFER TO S160 FOR ADDITIONAL SLAB REPAIR INFORMATION.

FOURTH FLOOR GENERAL NOTES:

- ALL DIMENSIONS FOR NEW OPENINGS ARE APPROXIMATE. VERIFY IN FIELD TO AVOID CONFLICTS WITH EXISTING CONSTRUCTION.
- THE DIMENSIONS OF ALL EXISTING OPENINGS SHOWN ARE TO BE VERIFIED IN THE FIELD.
- PENETRATIONS FOR INDIVIDUAL PLUMBING LOCATIONS NOT SHOWN ON THIS PLAN SHALL BE LOCATED TO AVOID CONCRETE JOISTS WHERE POSSIBLE. IF CONCRETE JOIST CANNOT BE AVOIDED AND MUST BE PENETRATED, PROVIDE REINFORCEMENT PER S140. DO NOT PENETRATE PRIMARY CONCRETE BEAMS UNDER ANY CIRCUMSTANCES.
- CONTRACTOR TO NOTIFY STRUCTURAL ENGINEER OF RECORD (SEOR) OF ANY UNDOCUMENTED PENETRATIONS, INCLUDING SIZE AND LOCATION.
- CONTRACTOR TO COORDINATE THE IMPROVEMENTS SHOWN ON THIS SHEET WITH ADDITIONAL CONCRETE REPAIRS ON S160 AND WITH WATER INTRUSION REPAIRS ON S401 - S408.
- A PATIENT LIFT TRACK SUPPORT SYSTEM IS TO BE INSTALLED ON THE UNDERSIDE OF THE FOURTH FLOOR. THE DESIGN AND LAYOUT IS BY OTHERS. REFER TO ARCHITECTURAL DRAWINGS FOR ADDITIONAL INFORMATION.
- THE ANCHORAGE OF THE PATIENT LIFT TRACK SUPPORT SYSTEM TO THE EXISTING CONCRETE STRUCTURE SHALL BE DESIGNED BY THE CONTRACTOR PER THE SYSTEM MANUFACTURER'S REQUIREMENTS.
- PROVIDE TRACK LIGHTING SUPPORTS WHERE REQUIRED BY ARCHITECT. REFER TO THE REFLECTED CEILING PLAN FOR LOCATIONS. REFER TO 6 AND 7/S142 FOR ATTACHMENT DETAILS.
- VISUALLY INSPECT EXISTING WELDS ON CROSS-BRACE LOCATIONS. NOTIFY RE FOR APPROVAL OF DEFECT REPAIR. INSPECT AND COAT WITH WITH PRIMER AFTER REPAIRING WELDS.
- VISUALLY INSPECT ALL EXISTING BOLTS. FULLY TIGHTEN ANY BOLTS THAT ARE LOOSE OR HAVE GAP SPACE BETWEEN FRAME AND BOLT HEAD.

CONFORMED SET
FOR CONSTRUCTION

Revisions: <table><tr><td> </td><td> </td></tr><tr><td> </td><td> </td></tr><tr><td> </td><td> </td></tr><tr><td> </td><td> </td></tr></table> Date:									CONSULTANT 623 26th Avenue Rock Island, IL 61201 T: 309.788.0673 F: 309.786.5967	ARCHITECT/ENGINEER OF RECORD 13605 1st Ave. N. #100 Plymouth, MN 55441 P 763.412.4000 F 763.412.4090 ae-mn.com Anderson Engineering of Minnesota, LLC Proj # 15090	STAMP 12/31/25	Office of Construction and Facilities Management U.S. Department of Veterans Affairs	Drawing Title FOURTH FLOOR FRAMING PLAN Approved:	Phase CONSTRUCTION DOCUMENTS FULLY SPRINKLERED	Project Title RENOVATE BUILDING 1 Location BILOXI, MISSISSIPPI Issue Date 05/12/2025 Checked MLA Drawn WHL	Project Number 520-317X Building Number 1 Drawing Number SF110 Dwg. 14 of 239

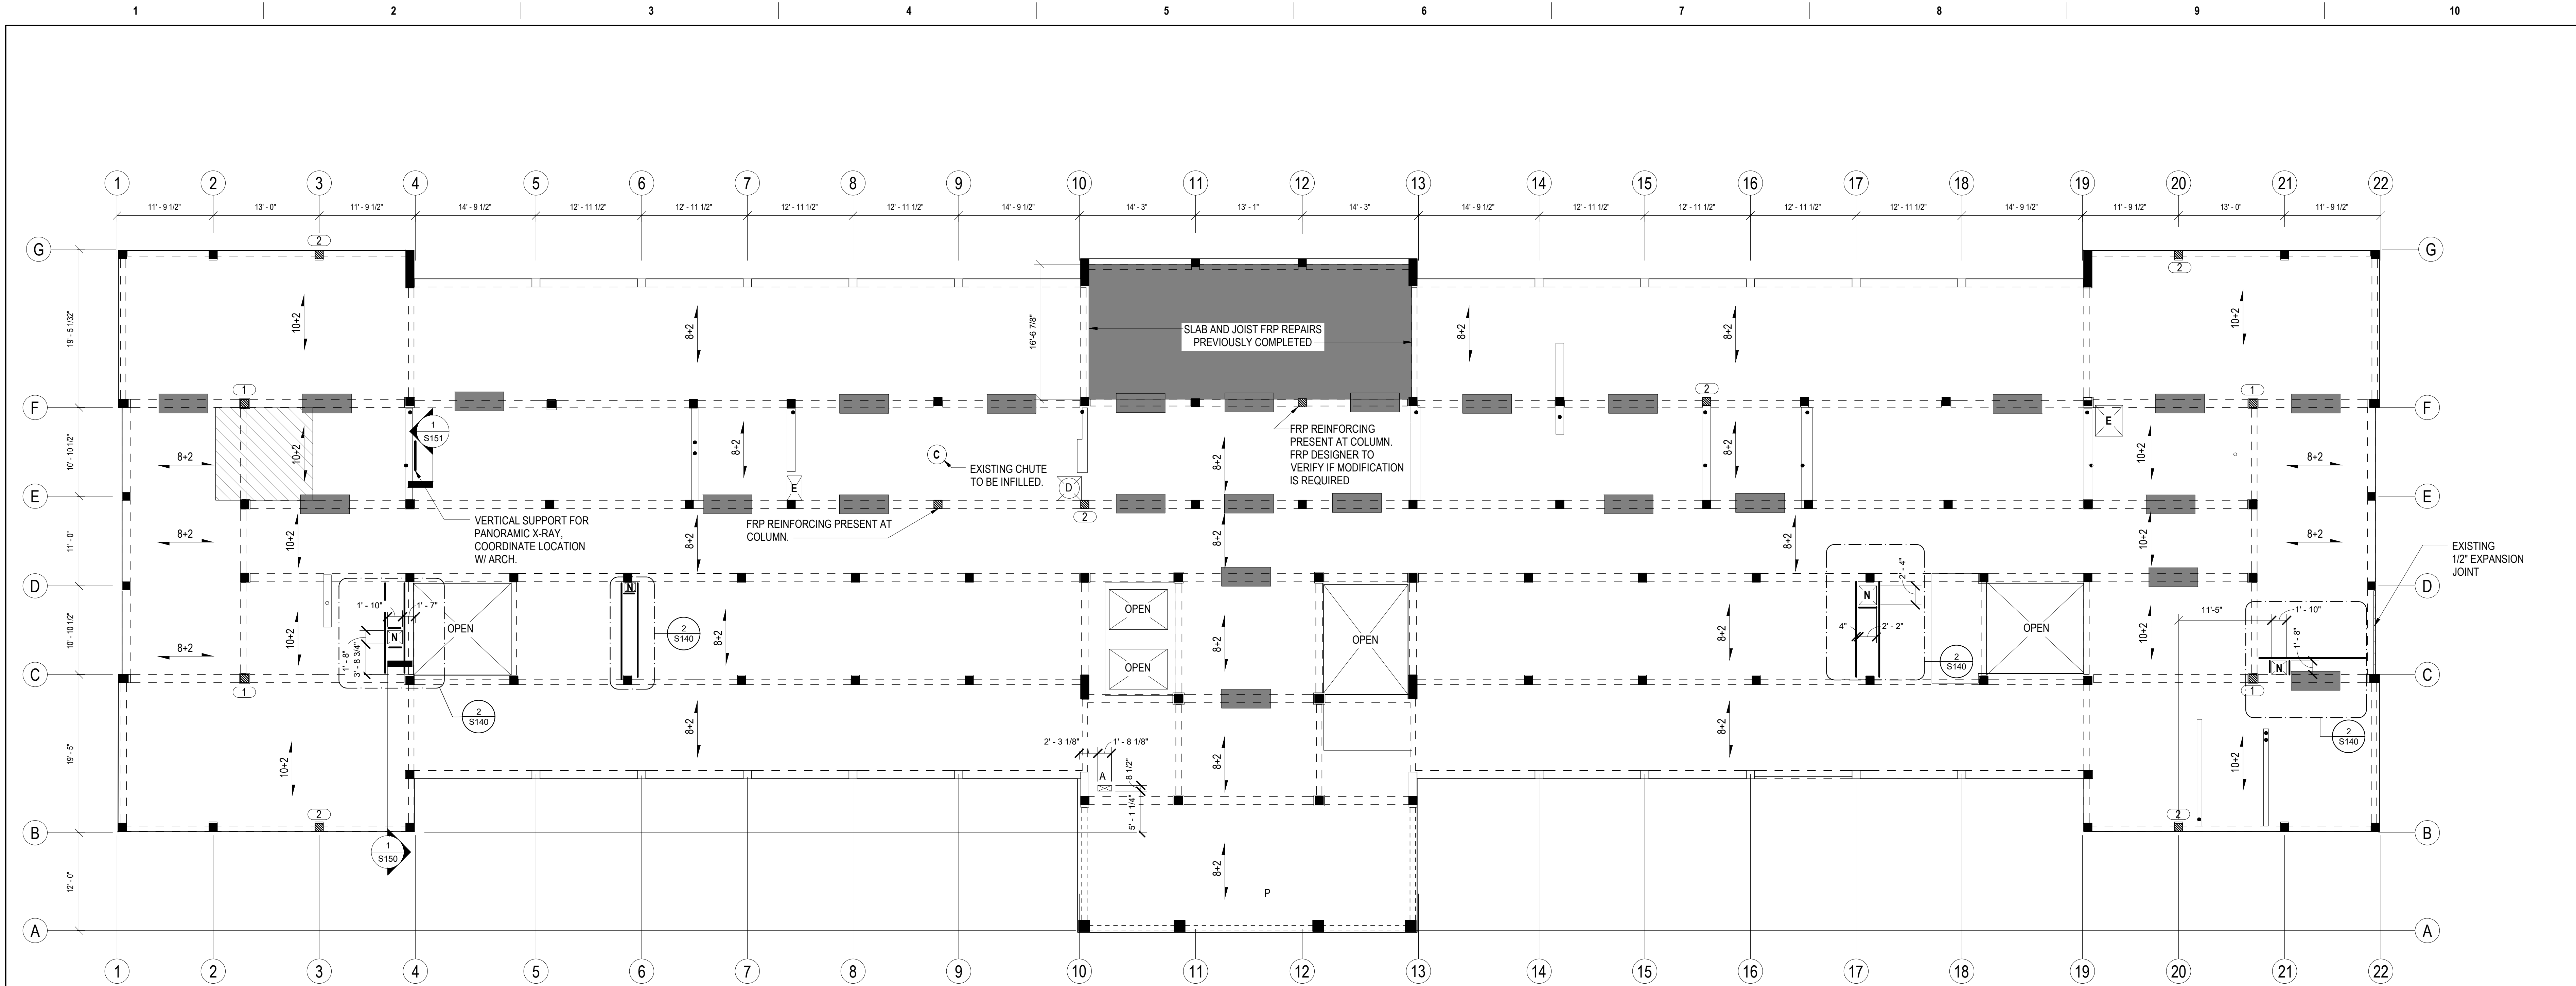

PLAN NORTH
1
FIFTH FLOOR FRAMING PLAN
1/8" = 1'-0"
FINISH FLOOR EL. 78'-6" (VIF)

LEGEND:


- INDICATES FRP BEAM REPAIRS PREVIOUSLY COMPLETED.
- PLUMBING CHASE THROUGH CONCRETE FLOOR, COORDINATE WITH MEP DRAWINGS. IF NEW CHASE IS PARALLEL TO CONCRETE JOIST SPANS, LOCATE OPENINGS TO AVOID CUTTING JOISTS.
IF NEW CHASE IS PERPENDICULAR TO CONCRETE JOIST SPANS, OR IF THE NEW OPENINGS OTHERWISE CUT THROUGH JOISTS, PROVIDE ADDITIONAL SUPPORT PER SHEET S140. REFER TO DETAILS 1, 2 OR 3 AS APPROPRIATE, DEPENDING ON HOW MANY ADJACENT JOISTS ARE CUT.
DO NOT CUT ANY PRIMARY BEAMS OR COLUMNS
- EXISTING JOIST SPANS TYP. FLOOR 2" CONCRETE SLAB OVER 8" JOIST (8"x21") @ 25" O.C., TYP., U.N.O.
- EXISTING JOIST SPANS TYP. FLOOR 2" CONCRETE SLAB OVER 10" JOIST (10"x21") @ 25" O.C., TYP., U.N.O.
- FOR BEAM LOCATIONS & SIZES REFERENCE EXISTING DRAWINGS OR VERIFY IN FIELD.
- AREAS OF DAMAGED CONCRETE, REFER TO S161.
- A = ACCESS HATCH.
- E = EXISTING EXHAUST TO REMAIN, FIELD VERIFY LOCATION AND SIZE.
- N = NEW EXHAUST, COORDINATE LOCATION WITH ARCH AND MEP DRAWINGS.
- C = EXISTING RUBBISH CHUTE TO BE INFILLED. REFER TO S161 FOR ADDITIONAL SLAB REPAIR INFORMATION.
- D = EXISTING RUBBISH CHUTE TO BE MODIFIED FOR NEW OPENING - REFER TO ARCHITECT FOR ADDITIONAL DETAILS.
- P = EXISTING PENETRATION THROUGH SLAB TO BE INFILLED. REFER TO S161 FOR ADDITIONAL SLAB REPAIR INFORMATION.
- 12"x12" COLUMN WITH (4) #5 VERTICALS. (E) FRP REINFORCING PRESENT AT COLUMN. FRP DESIGNER TO VERIFY IF FRP MODIFICATION IS REQUIRED. COLUMN TO BE REINFORCED BETWEEN 5TH FLOOR AND ATTIC FOR ADDITIONAL 12% MOMENT CAPACITY.
- 12"x12" COLUMN WITH (4) #5 VERTICALS. COLUMN TO BE REINFORCED BETWEEN 5TH FLOOR AND ATTIC FOR ADDITIONAL 14% MOMENT CAPACITY.

FIFTH FLOOR GENERAL NOTES:

- ALL DIMENSIONS FOR NEW OPENINGS ARE APPROXIMATE. VERIFY IN FIELD TO AVOID CONFLICTS WITH EXISTING CONSTRUCTION.
- THE DIMENSIONS OF ALL EXISTING OPENINGS SHOWN ARE TO BE VERIFIED IN THE FIELD.
- PENETRATIONS FOR INDIVIDUAL PLUMBING LOCATIONS NOT SHOWN ON THIS PLAN SHALL BE LOCATED TO AVOID CONCRETE JOISTS WHERE POSSIBLE. IF CONCRETE JOIST CANNOT BE AVOIDED AND MUST BE PENETRATED, PROVIDE REINFORCEMENT PER 1/S140. DO NOT PENETRATE PRIMARY CONCRETE BEAMS UNDER ANY CIRCUMSTANCES.
- CONTRACTOR TO NOTIFY STRUCTURAL ENGINEER OF RECORD (SEOR) OF ANY UNDOCUMENTED PENETRATIONS, INCLUDING SIZE AND LOCATION.
- CONTRACTOR TO COORDINATE THE IMPROVEMENTS SHOWN ON THIS SHEET WITH ADDITIONAL CONCRETE REPAIRS ON S161 AND WITH WATER INTRUSION REPAIRS ON S401 - S406.
- A PATIENT LIFT TRACK SUPPORT SYSTEM IS TO BE INSTALLED ON THE UNDERSIDE OF THE FIFTH FLOOR. THE DESIGN AND LAYOUT IS BY OTHERS. REFER TO ARCHITECTURAL DRAWINGS FOR ADDITIONAL INFORMATION.
- THE ANCHORAGE OF THE PATIENT LIFT TRACK SUPPORT SYSTEM TO THE EXISTING CONCRETE STRUCTURE SHALL BE DESIGNED BY THE CONTRACTOR PER THE SYSTEM MANUFACTURER'S REQUIREMENTS.
- PROVIDE TRACK LIGHTING SUPPORTS WHERE REQUIRED BY ARCHITECT. REFER TO THE REFLECTED CEILING PLAN FOR LOCATIONS. REFER TO 6 AND 7/S142 FOR ATTACHMENT DETAILS.
- VISUALLY INSPECT EXISTING WELDS ON CROSS-BRACE LOCATIONS. NOTIFY RE FOR APPROVAL OF DEFECT REPAIR. INSPECT AND COAT WITH WITH PRIMER AFTER REPAIRING WELDS.
- VISUALLY INSPECT ALL EXISTING BOLTS. FULLY TIGHTEN ANY BOLTS THAT ARE LOOSE OR HAVE GAP SPACE BETWEEN FRAME AND BOLT HEAD.

CONFORMED SET
FOR CONSTRUCTION

--	--	

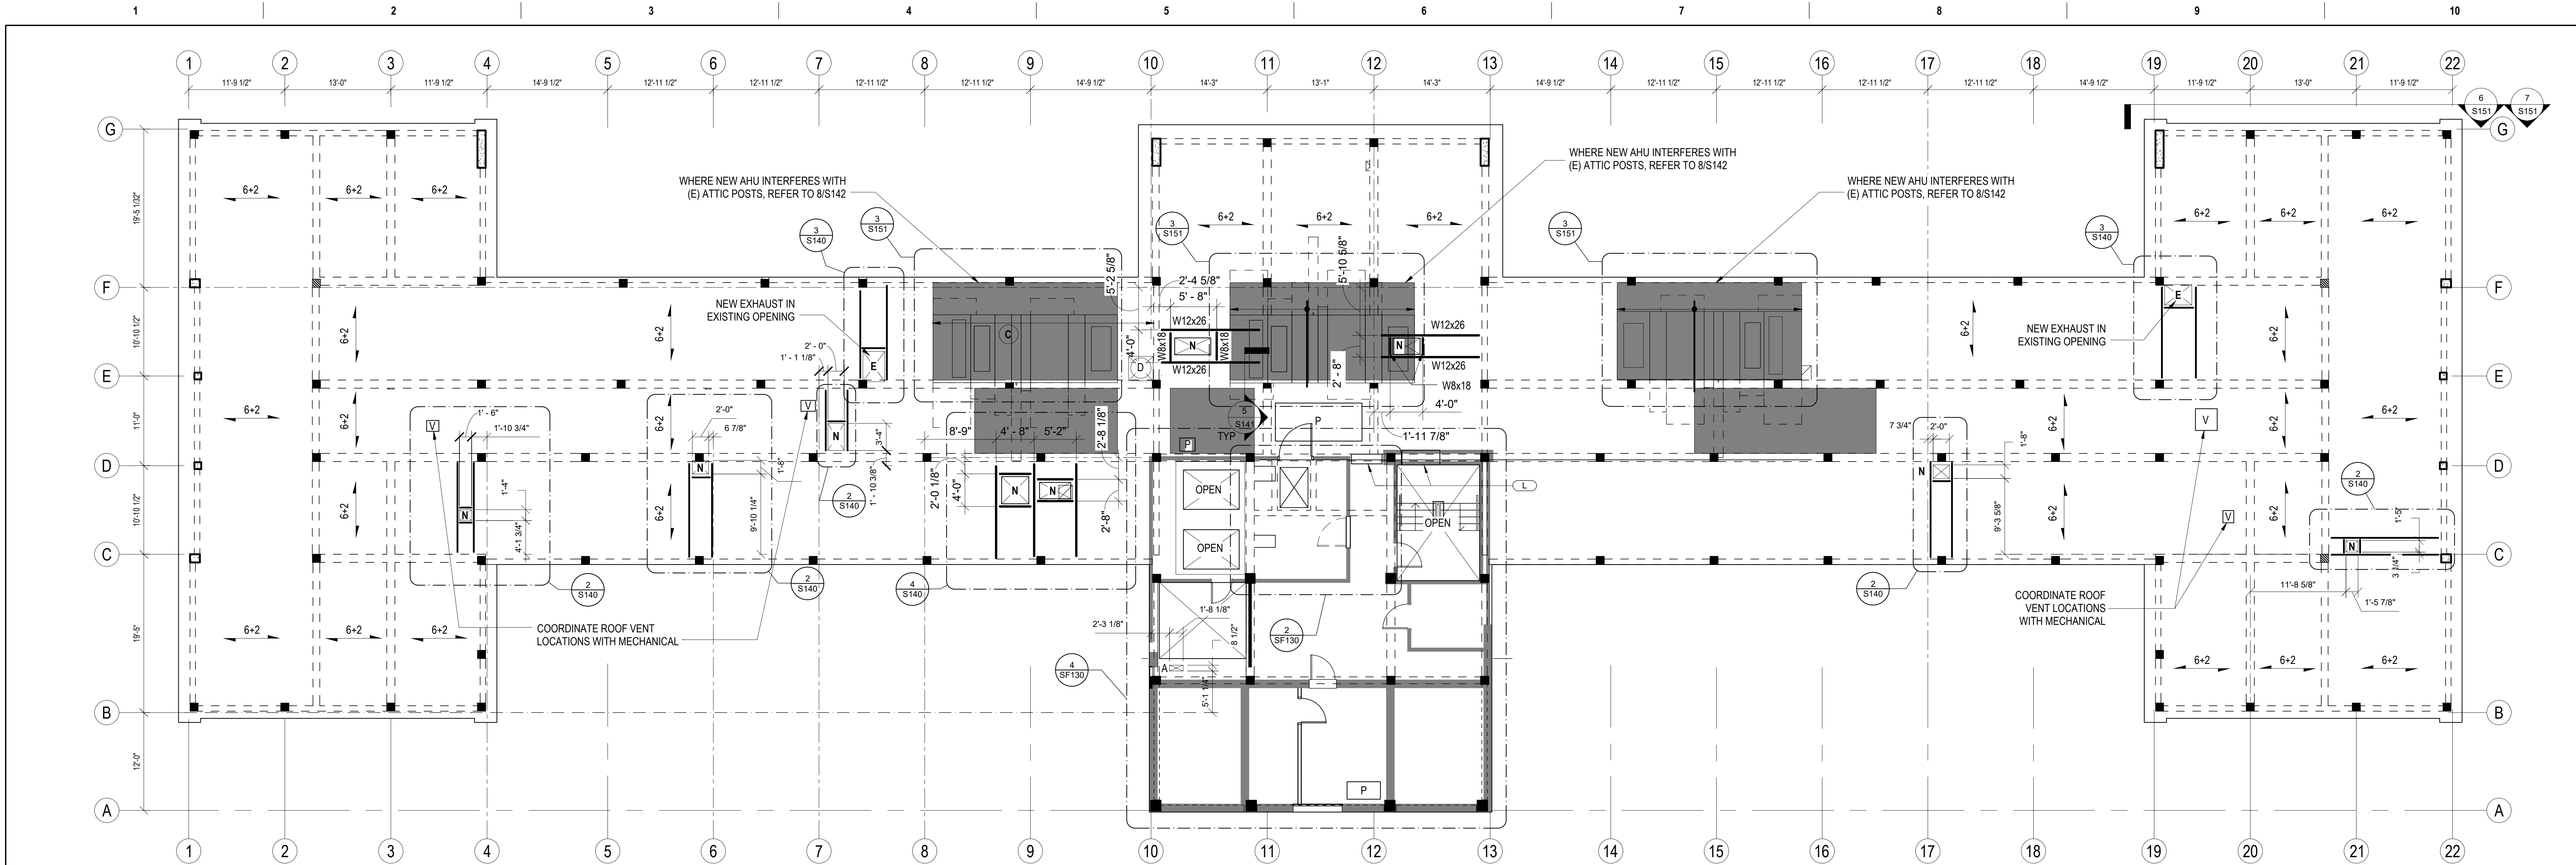

PLAN NORTH
1 ATTIC FRAMING PLAN
1/8" = 1'-0"
FINISH FLOOR EL. 92'-5" (VIF)

LEGEND:


SHADED AREA INDICATES REGION OF JOIST STRENGTHENING PREVIOUSLY COMPLETED FOR AHU REPLACEMENT.

6+2 = ALL EXISTING ATTIC FLOORS ARE 2" SLAB ON 6" JOISTS @ 25" O.C. (2'+6")


- A = ACCESS HATCH
E = EXISTING EXHAUST TO REMAIN, FIELD VERIFY LOCATION AND SIZE
N = NEW EXHAUST
C = EXISTING RUBBISH CHUTE TO BE INFILLED. REFER TO S162 FOR ADDITIONAL SLAB REPAIR INFORMATION.
D = EXISTING RUBBISH CHUTE TO BE MODIFIED FOR NEW OPENING - REFER TO ARCHITECT FOR ADDITIONAL DETAILS.
P = EXISTING PENETRATION THROUGH SLAB TO BE INFILLED. REFER TO SHEETS S162 FOR ADDITIONAL SLAB REPAIR INFORMATION.
V = NEW OPENING FOR ROOF VENT ABOVE, COORDINATE LOCATION WITH ARCHITECT AND MECHANICAL DRAWINGS. REFER TO S151.
L = NEW LINTEL IN EXISTING MASONRY WALL. REFER TO ARCHITECT FOR OPENING SIZE AND LOCATION. REFER TO GENERAL NOTES AND SCHEDULE ON SHEET S001 FOR LINTEL SIZE.

ATTIC GENERAL NOTES:

- ALL DIMENSIONS FOR NEW OPENINGS ARE APPROXIMATE. VERIFY IN FIELD TO AVOID CONFLICTS WITH EXISTING CONSTRUCTION.
- THE DIMENSIONS OF ALL EXISTING OPENINGS SHOWN ARE TO BE VERIFIED IN THE FIELD.
- THE DISTRIBUTED WEIGHT OF NEW MECHANICAL EQUIPMENT AND ASSOCIATED STRUCTURAL SUPPORT SHALL NOT EXCEED 150 PSF.
- REFER TO ARCHITECTURAL AND MECHANICAL ROOF PLANS FOR LOCATIONS OF EXISTING OPENINGS AND EQUIPMENT TO BE REMOVED. OPENINGS LARGER THAN 16'x16" MAY BE PATCHED PER DETAIL S151.
- A PATIENT LIFT TRACK SUPPORT SYSTEM IS TO BE INSTALLED ON THE UNDERSIDE OF THE ATTIC FLOOR. THE DESIGN AND LAYOUT IS BY OTHERS. REFER TO ARCHITECTURAL DRAWINGS FOR ADDITIONAL INFORMATION.
- THE ANCHORAGE OF THE PATIENT LIFT TRACK SUPPORT SYSTEM TO THE EXISTING CONCRETE STRUCTURE SHALL BE DESIGNED BY THE CONTRACTOR PER THE SYSTEM MANUFACTURER'S REQUIREMENTS.
- PROVIDE TRACK LIGHTING SUPPORTS WHERE REQUIRED BY ARCHITECT. REFER TO THE REFLECTED CEILING PLAN FOR LOCATIONS. REFER TO 6 AND 7/S142 FOR ATTACHMENT DETAILS.

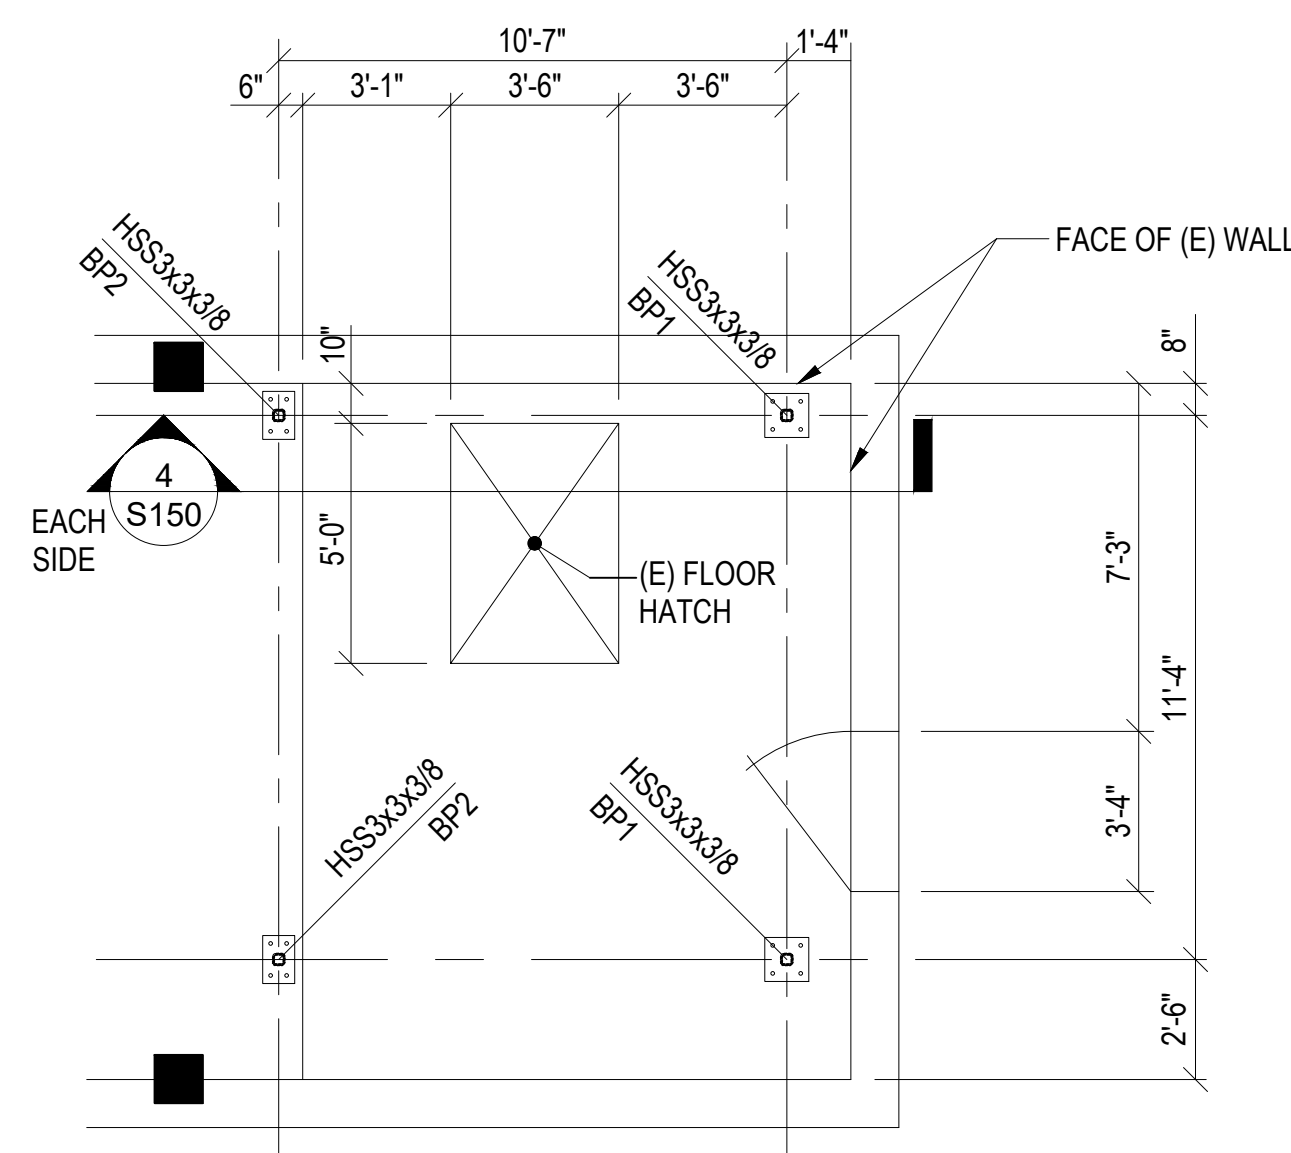


PLAN NORTH
2 HOIST PLAN BASE DETAIL
1/4" = 1'-0"

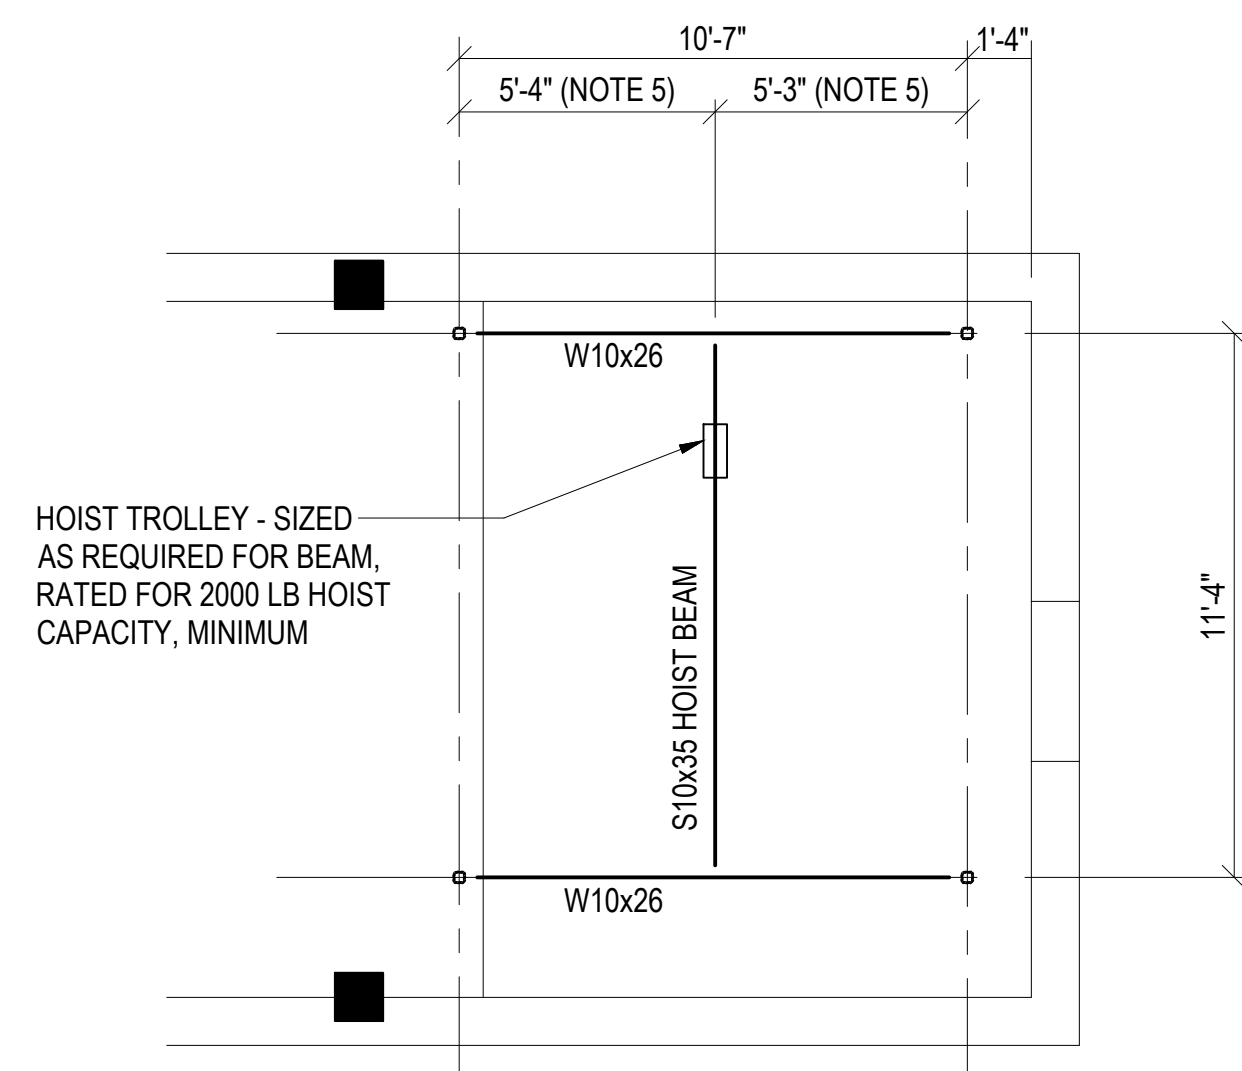

PLAN NORTH
3 HOIST FRAMING PLAN DETAIL
1/4" = 1'-0"

- EXISTING ROOF OPENING AT OLD CHIMNEY, TO BE PATCHED AS FOLLOWS:
- REMOVE EXISTING COVERING AND CLEAN STRUCTURE TO RECEIVE NEW ATTACHMENT.
 - VERIFY SIZE OF OPENING DOES NOT EXCEED 9'-0"x9'-0".
 - PLACE NEW GALVANIZED 3" x 18 GA METAL ROOF DECK, WITH MINIMUM 8" OF BEARING ON ALL SIDES.
 - FASTEN PERIMETER OF ROOF DECK TO CONCRETE OR MASONRY WITH 3/16" TITEN SCREWS @ 6" O.C. (1 3/4" EMBED). SCREWS TO HAVE MINIMUM EDGE DISTANCE OF 4".
 - IF EXISTING CONSTRUCTION DOES NOT PERMIT INSTALLATION AS DESCRIBED ABOVE, CONTACT THE STRUCTURAL ENGINEER OF RECORD (SEOR) FOR ADDITIONAL INSTRUCTIONS.

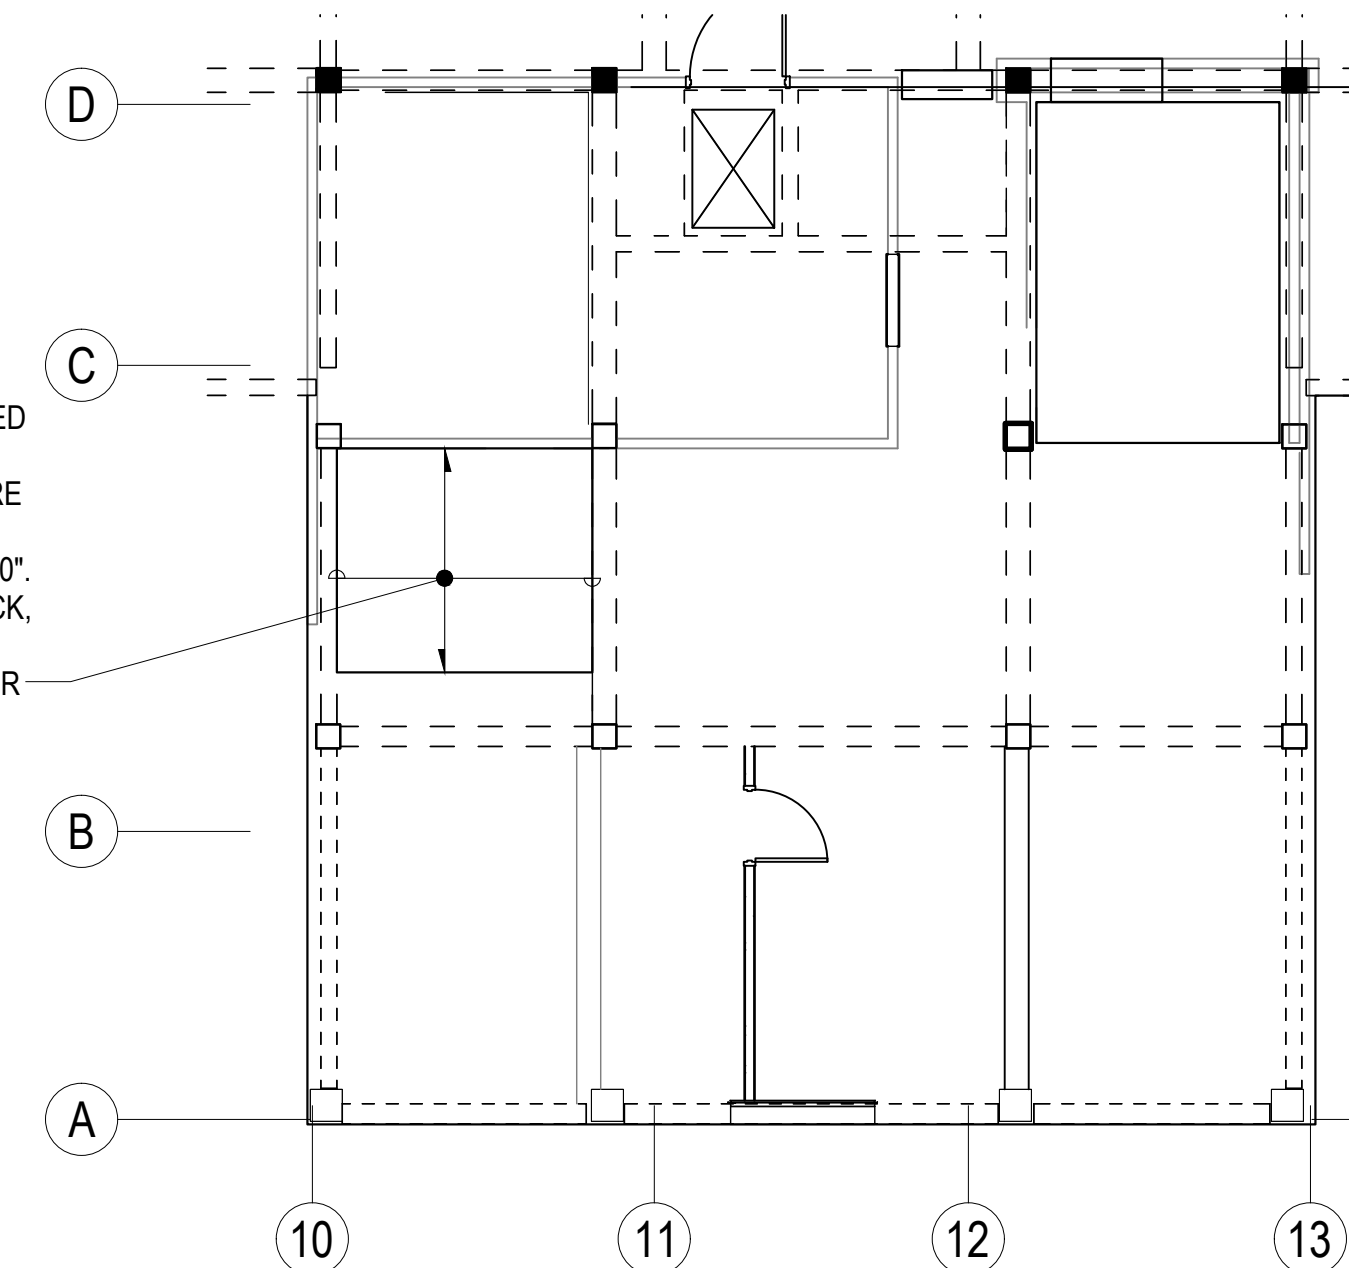

PLAN NORTH
4 PARTIAL ROOF PLAN
1/8" = 1'-0"


NOTES:

- COORDINATE LAYOUT OF HOIST WITH ARCHITECTURAL DRAWINGS. CONTRACTOR TO VERIFY EXISTING CLEARANCES AND ROOM HEIGHT PRIOR TO FABRICATING HOIST.
- MAXIMUM HOIST LOAD = 2000 LBS. PAINT NOTICE OF RATING ON HOIST BEAM IN LARGE LETTERS.
- PLACE HOIST BEAM CENTERED OVER EXISTING OPENING.
- REFER TO SHEET S150 FOR BASE PLATE.
- FIELD VERIFY EXISTING CONDITIONS SO THAT HOIST BEAM IS CENTERED OVER (E) HATCH.



ADDENDUM #1	05/14/2024
Revisions:	Date:

CONSULTANT IMEG 623 26th Avenue Rock Island, IL 61201 T: 309.788.0673 F: 309.786.5967	ARCHITECT/ENGINEER OF RECORD ANDERSON 13605 1st Ave. N. #100 Plymouth, MN 55441 P 763.412.4000 F 763.412.4090 ae-mn.com Anderson Engineering of Minnesota, LLC Proj # 15090	STAMP 5/17/25 LEATHER HEIDEN ENGINEER STATE OF MINNESOTA EX 12/31/25	Office of Construction and Facilities Management VA U.S. Department of Veterans Affairs	Drawing Title ATTIC FRAMING PLAN Approved:	Phase CONSTRUCTION DOCUMENTS FULLY SPRINKLERED	Project Title RENOVATE BUILDING 1 Location BILOXI, MISSISSIPPI Issue Date 05/12/2025 Checked MLA Drawn WHL	Project Number 520-317X Building Number 1 Drawing Number SF130 Dwg. 16 of 239
--	--	---	--	--	---	---	---


CONFORMED SET
FOR CONSTRUCTION

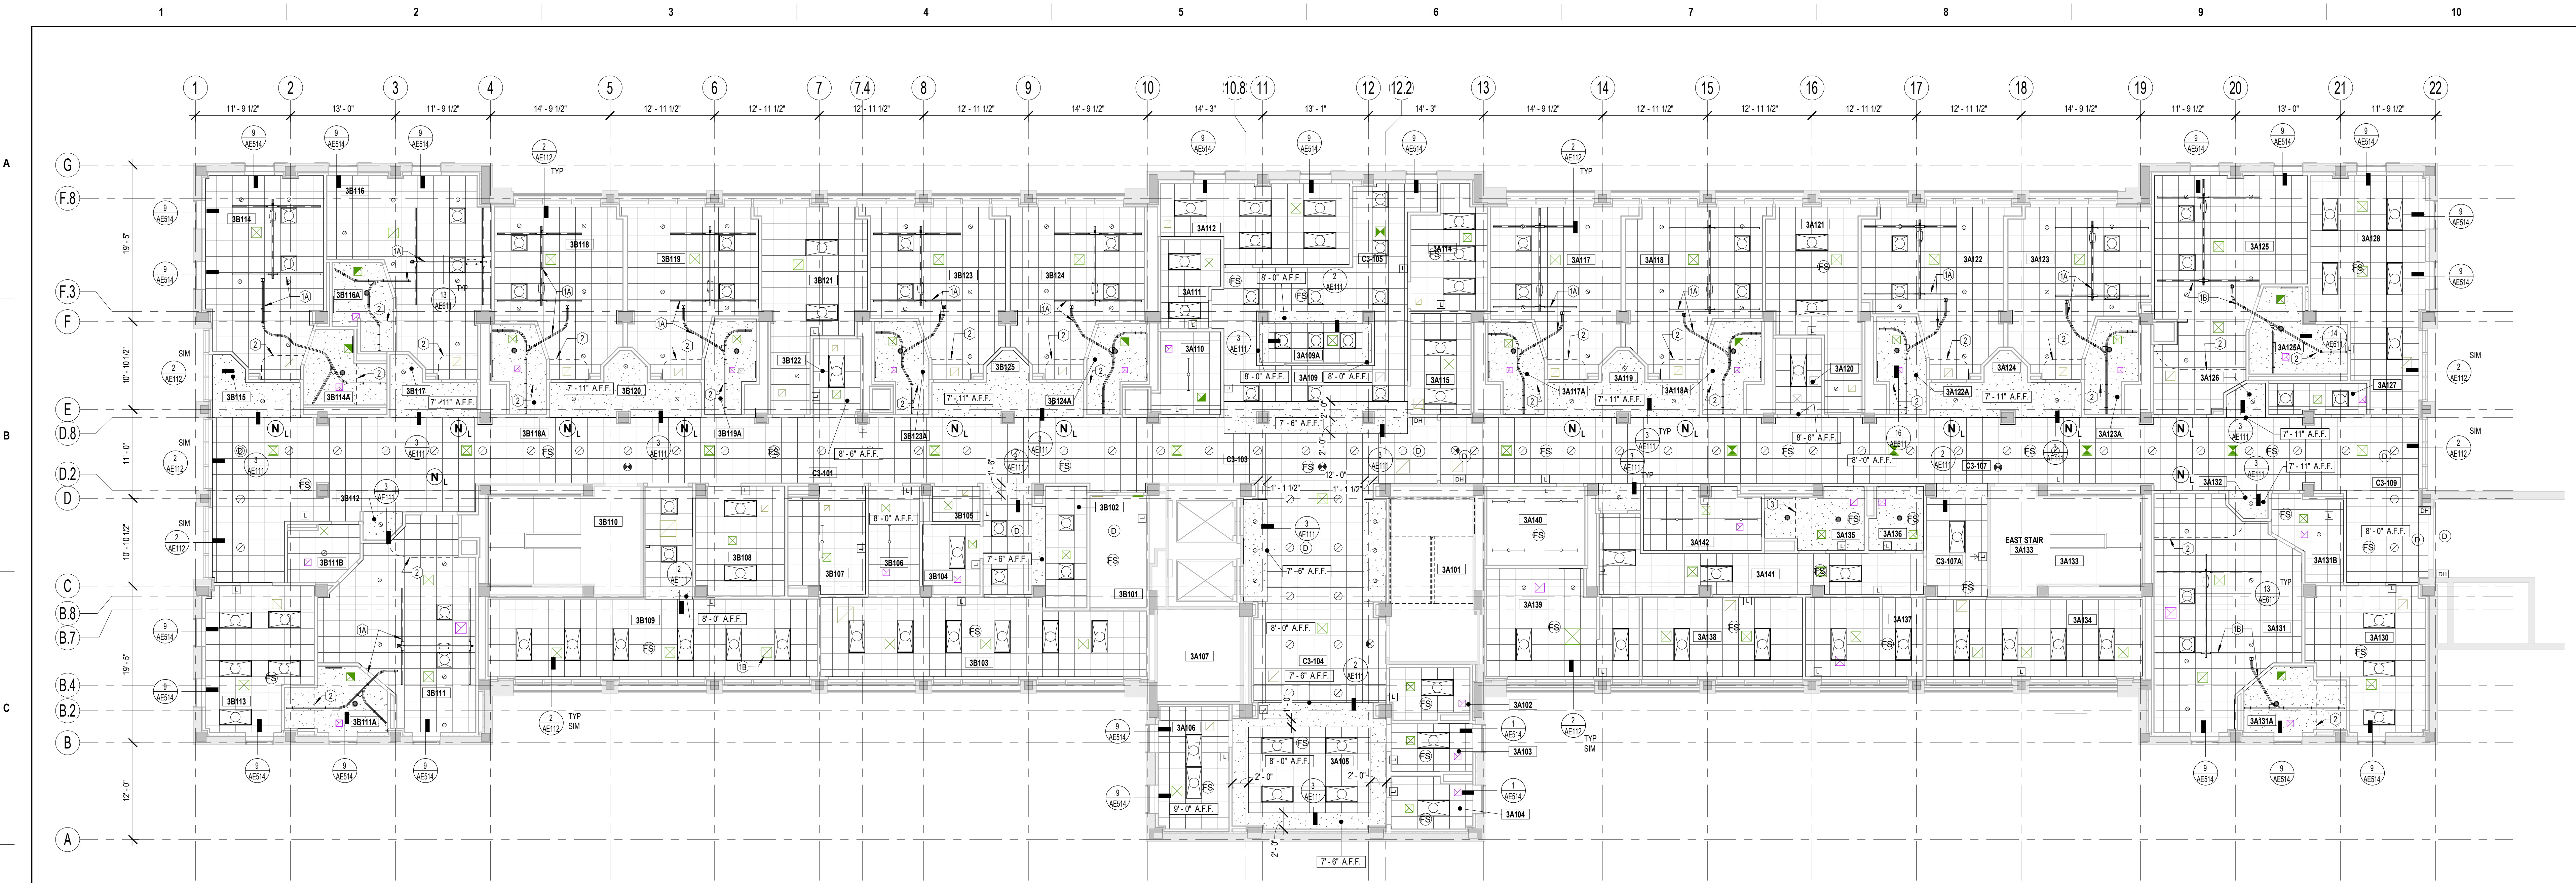

1 3RD FLOOR REFLECTED CEILING PLAN
AE111 1/8\" = 1'-0"

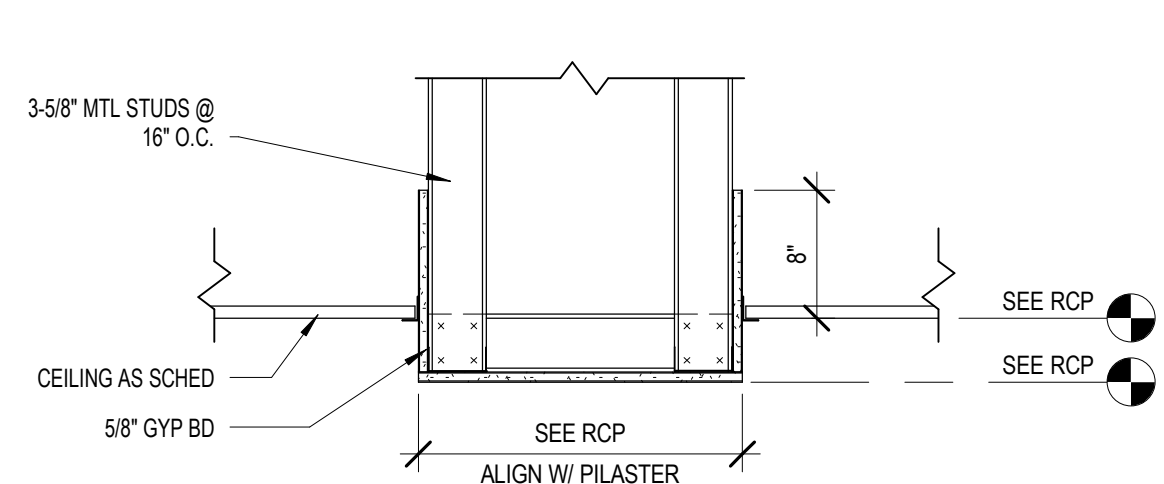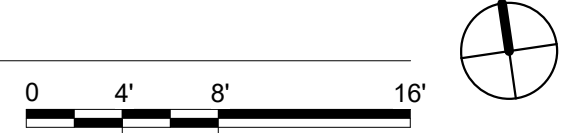

2 TYPICAL CORRIDOR FURDOWN
AE111 1\" = 1'-0"

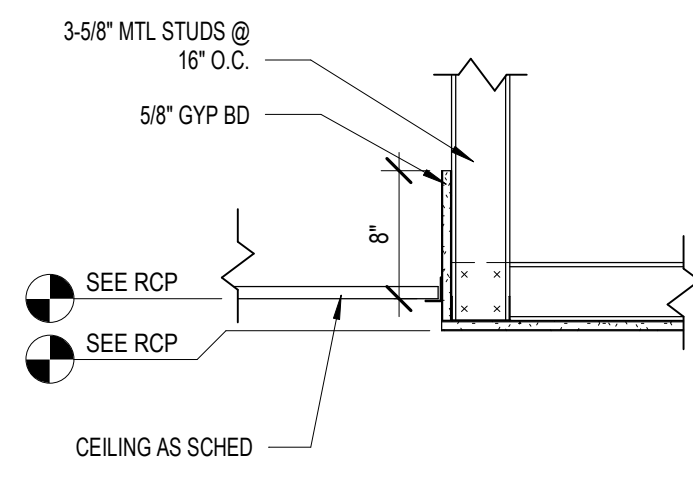

3 TYPICAL CEILING TRANSITION
AE111 1\" = 1'-0"

RCP LEGEND

	2X2 LAY IN TILE		TROFFER LIGHT FIXTURE, SEE ELEC.
	GYP BOARD		DOWNLIGHT RECESSED LIGHT FIXTURE, SEE ELEC.
	EXP STRUCT		DOWNLIGHT STRIP LIGHT FIXTURE, SEE ELEC.
	8'-0\" AFF. CEILING HEIGHT		CEILING MOUNTED SPEAKER
	EXIT LIGHT, SEE ELEC.		MECH DIFFUSERS/GRILLES, SEE MECH.
	LIFT TRACK		FIRE ALARM CEILING MOUNTED SPEAKER, SEE ELEC.
	LIGHT FIXTURE, SURFACE MOUNT, SEE ELEC.		SMOKE DETECTOR
	STRIP LIGHT FIXTURE, SEE ELEC.		PRIVACY CURTAIN OR SHOWER CURTAIN
	CORRIDOR LIGHT VISUAL INDICATOR FOR NURSE CALL, SEE TELECOM		WALL MOUNTED FIRE ALARM DEVICES - DOOR HOLD OPEN
	WALL MOUNTED FIRE ALARM DEVICES - STROBE, SEE ELEC.		WALL MOUNTED FIRE ALARM DEVICES - SPEAKER STROBE, SEE ELEC.

RCP GENERAL NOTES

- CONTRACTOR IS TO FIELD VERIFY ALL DIMENSIONS AND CONDITIONS.
- UPON DISCOVERY OF ANY DISCREPANCIES BETWEEN DRAWINGS AND DEPICTING EXISTING CONDITIONS OR UPON DISCOVERY OF UNKNOWN CONDITIONS DETRIMENTAL TO THE COMPLETION OF THE WORK AS INDICATED IN THE DOCUMENTS, THE CONTRACTOR SHALL IMMEDIATELY NOTIFY ARCHITECT AND THE RESIDENT ENGINEER, IN WRITING, OF THE CONDITION IN QUESTION BEFORE PROCEEDING WITH WORK IN THAT AREA. SEE DETAIL 16/AE611
- WHERE LAY-IN CEILING UNITS LESS THAN 6 INCHES WIDE OCCUR AT EDGES OF ROOM WITH 24X24 INCH PATTERN PROVIDE 24X48 INCH PANELS CUT TO EXTEND TO WALL ELIMINATING THE TEE NEAR THE WALL.
- THE PROPER LAYOUT OF THE RCP IS A COMBINATION OF ELECTRICAL & MECHANICAL PLANS AND THE CEILING FINISH CHOSEN. COORDINATION IS REQUIRED PRIOR TO INSTALLATION OF THE CEILING, LIGHT FIXTURES, DIFFUSERS, ETC. COORDINATION/RESOLUTION TO CEILING CONFLICTS ARE TO BE APPROVED BY RESIDENT ENGINEER.
- SEE MECHANICAL AND ELECTRICAL SHEETS TO VERIFY SIZE, TYPE, NUMBER AND LOCATIONS OF FIXTURES.
- ALL LIGHTS TO BE CENTERED WITHIN 2X2 GRID (TYPICAL); ALL 2X2 GRIDS TO BE CENTERED WITHIN ROOM (TYPICAL).
- PROVIDE PAINTABLE ACCESS PANELS IN GYP BD CEILINGS AS REQ'D FOR ACCESS TO MECH & PLUMBING EQUIP. SEE MECH & PLUMBING FOR LOCATIONS.
- ALL SUSPENDED ACP AND GYPSUM BOARD CEILING HEIGHTS ARE AT 9'-0\" AFF. U.N.O. ALL GYPSUM BOARD SOFFITS ARE AT 7'-11\" AFF. U.N.O.

RCP KEY NOTES

- PATIENT LIFT TRACK(V), 550W RE. SPECIALTY EQUIPMENT DRAWINGS (LIFTS), SEE DETAIL 13/AE611, 14/AE611, AND 19/AE611
- PATIENT LIFT TRACK(V), 770W RE. SPECIALTY EQUIPMENT DRAWINGS (LIFTS), SEE DETAIL 13/AE611, 14/AE611, AND 19/AE611
- PRIVACY CURTAIN & TRACK
- SHOWER CURTAIN & ROD
- PROVIDE STEEL SUPPORT ABOVE SUSPENDED CEILING FOR CEILING MOUNTED TOILET PARTITIONS. SEE DETAIL 15/AE611
- CEILING TRACK FOR DENTAL LIGHT
- PROVIDE REINFORCED LENGTHS OF CEILING TRACKS AS REQUIRED TO ALLOW FOR REMOVAL OF 6' X 6' AREA OF ACT FOR ACCESS/USE OF THE ATTIC HATCH. SEE 11AE110.

**CONFORMED SET
FOR CONSTRUCTION**

NO.	REVISIONS	DATE

CONSULTANT




623 26th Avenue
Rock Island, IL 61201
T: 309.788.9673
F: 309.786.5967

ARCHITECT/ENGINEER OF RECORD

THOMAS OLESAK, ARCHITECT
MS Lic # 5505

1050 HOYT AVE WEST ST PAUL, MN 55117
952-451-0460

STAMP

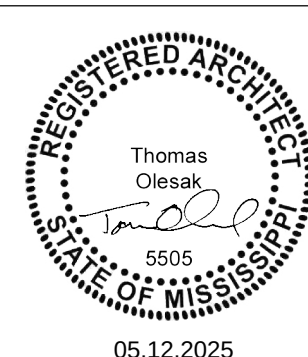

Office of
Construction
and Facilities
Management



U.S. Department of
Veterans Affairs

Drawing Title
**3RD FLOOR REFLECTED CEILING
PLAN**

Approved:

Phase
**CONSTRUCTION
DOCUMENTS**

FULLY SPRINKLERED

Project Title
RENOVATE BUILDING 1

Location
BILOXI, MISSISSIPPI

Issue Date
05/12/2025

Checked
LA


Drawn
CD,PC

Project Number
520-317X



Building Number
1

Drawing Number
AE111


Dwg. 75 of 239

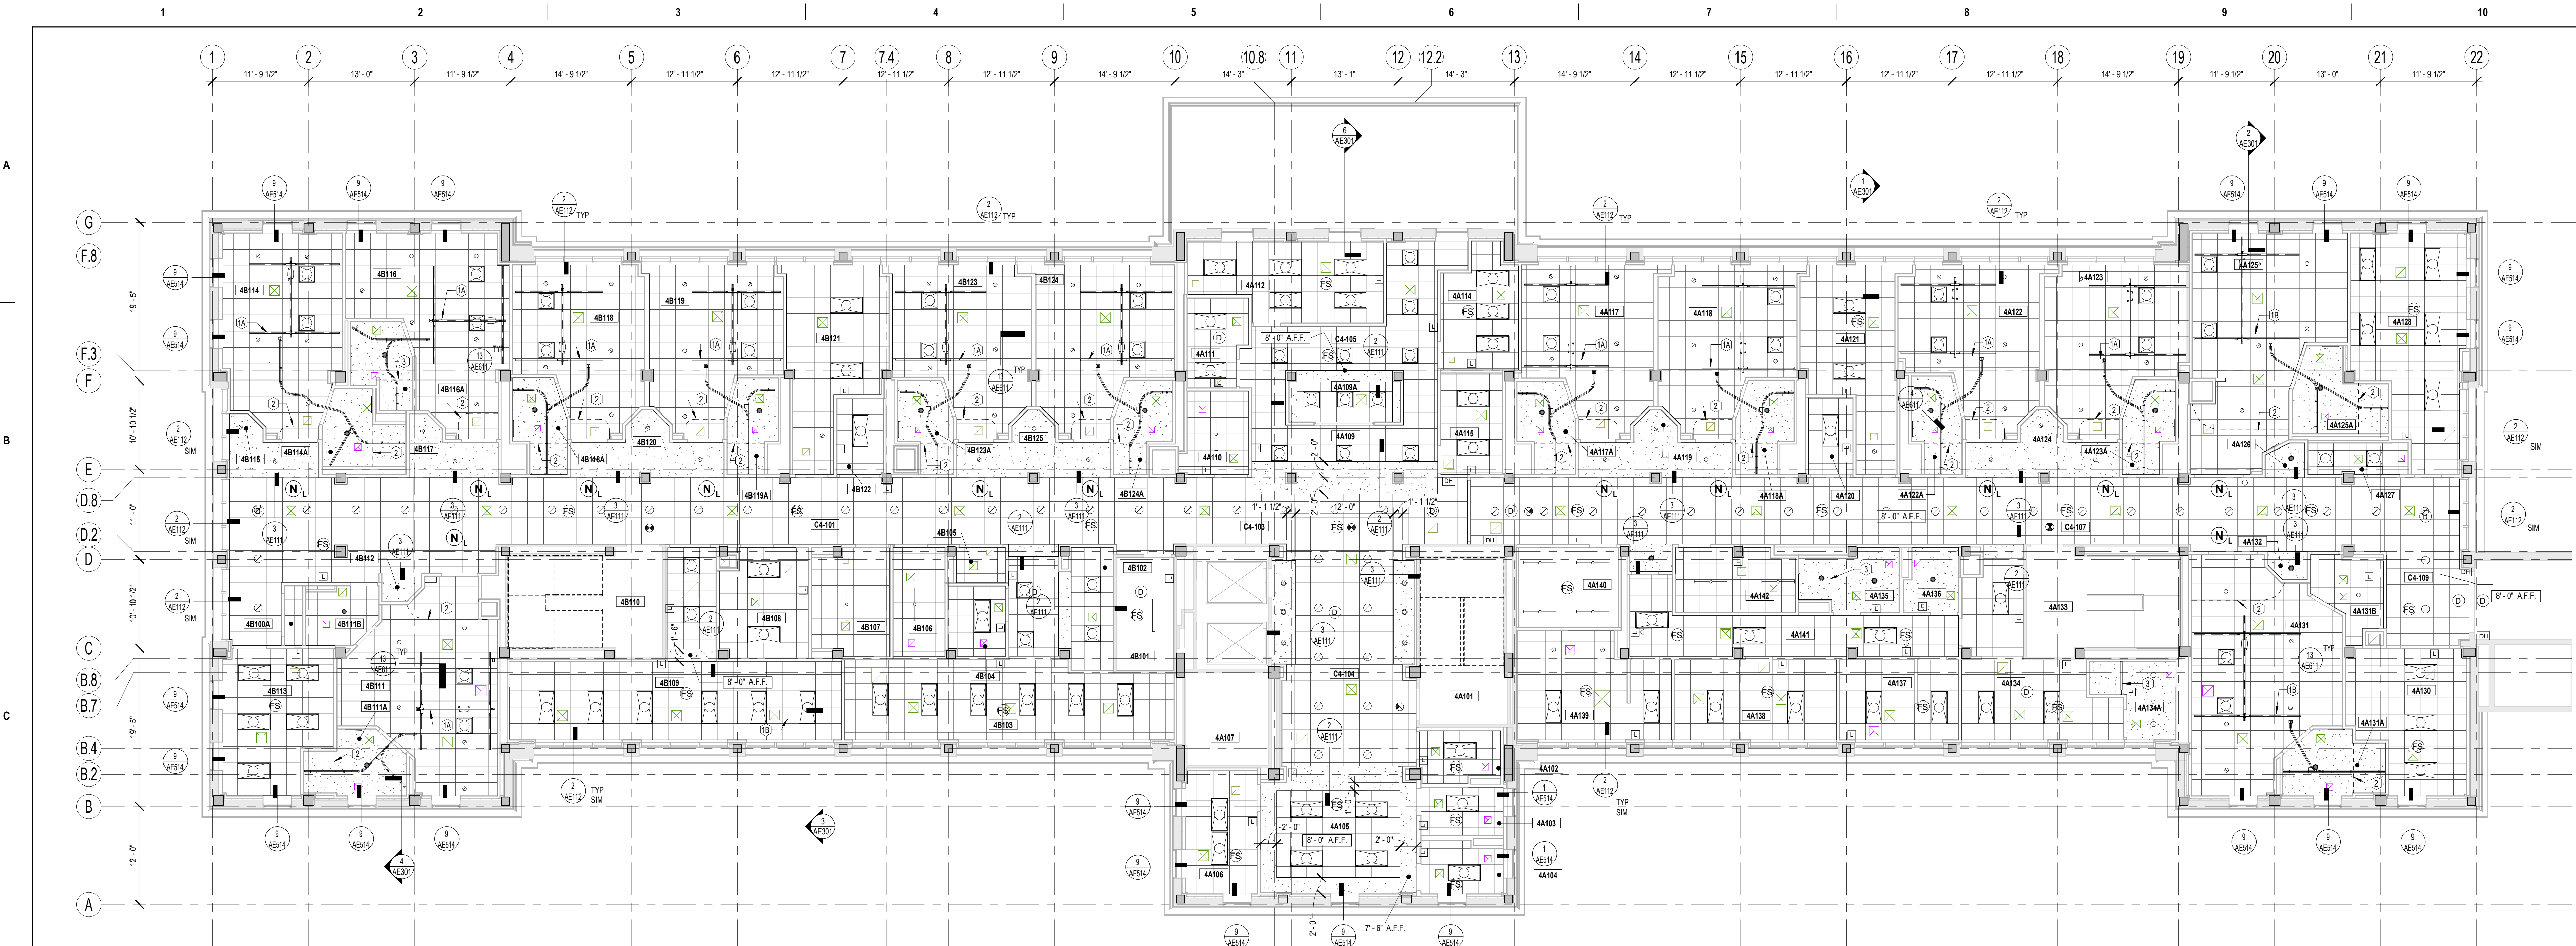

1 4TH FLOOR REFLECTED CEILING PLAN
1/8" = 1'-0"

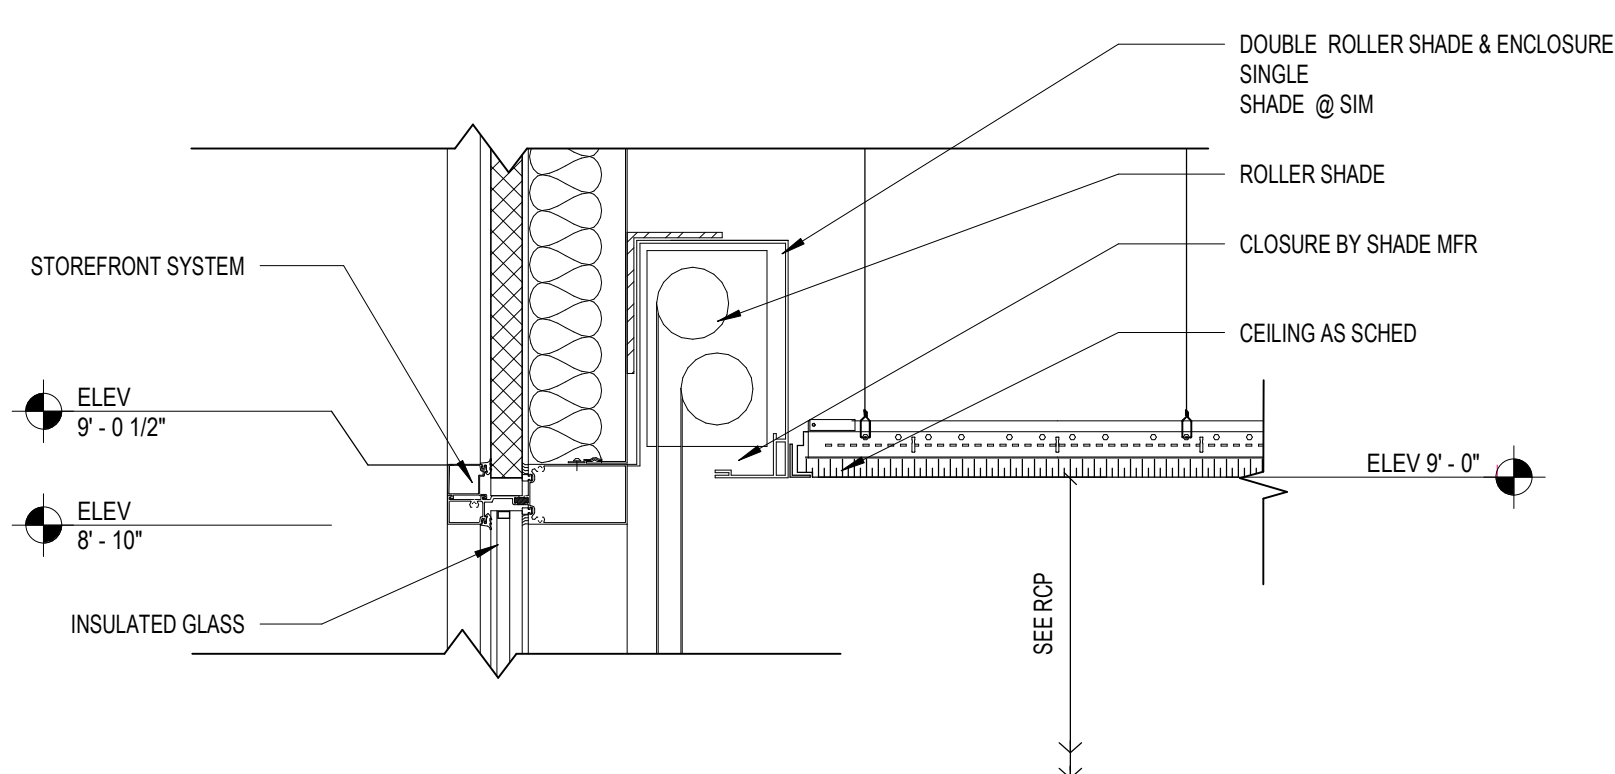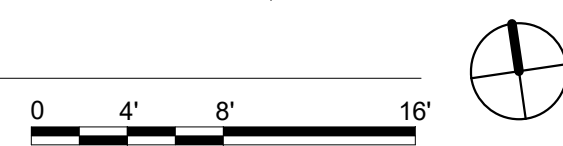

2 ACT CONNECTION AT DOUBLE ROLLER SHADE
1 1/2" = 1'-0"

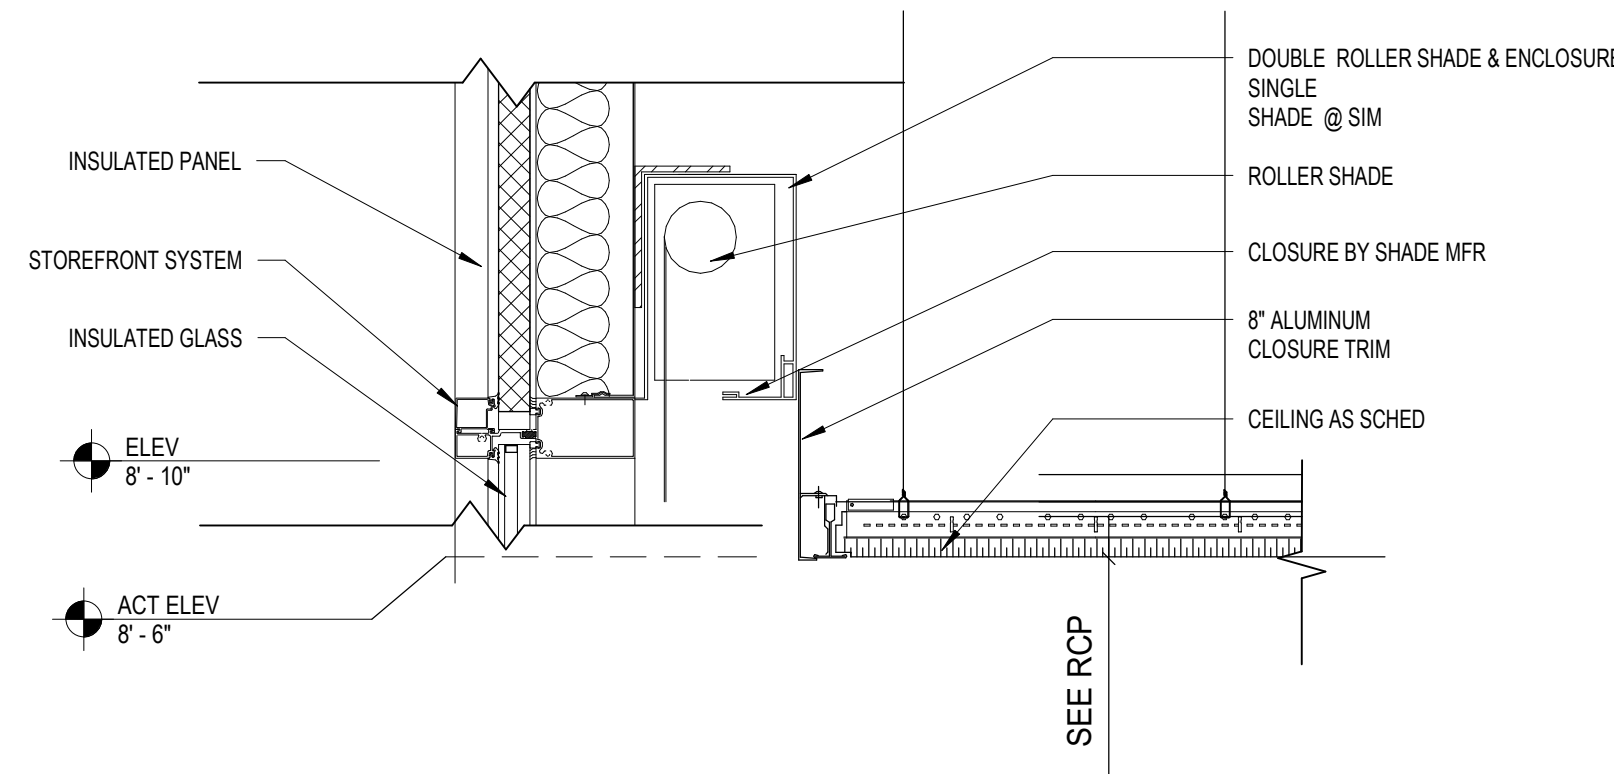

3 ACT CONNECTION AT SINGLE ROLLER SHADE
1 1/2" = 1'-0"


RCP LEGEND	
	2X2 LAY IN TILE
	GYP BOARD
	EXP STRUCT
	8' - 0" A.F.F. CEILING HEIGHT
	EXIT LIGHT, SEE ELEC.
	LIFT TRACK
	LIGHT FIXTURE SURFACE MOUNT, SEE ELEC.
	STRIP LIGHT FIXTURE, SEE ELEC.
	CORRIDOR LIGHT VISUAL INDICATOR FOR NURSE CALL, SEE TELECOM
	WALL MOUNTED FIRE ALARM DEVICES - STROBE, SEE ELEC.
	TROFFER LIGHT FIXTURE, SEE ELEC.
	DOWNLIGHT RECESSED LIGHT FIXTURE, SEE ELEC.
	DOWNLIGHT STRIP LIGHT FIXTURE, SEE ELEC.
	CEILING MOUNTED SPEAKER
	MECH DIFFUSERS/GRILLES - SEE MECH.
	FIRE ALARM CEILING MOUNTED SPEAKER, SEE ELEC.
	SMOKE DETECTOR
	PRIVACY CURTAIN OR SHOWER CURTAIN
	WALL MOUNTED FIRE ALARM DEVICES - DOOR HOLD OPEN
	WALL MOUNTED FIRE ALARM DEVICES - SPEAKER STROBE, SEE ELEC.

RCP GENERAL NOTES	
1.	CONTRACTOR IS TO FIELD VERIFY ALL DIMENSIONS AND CONDITIONS.
2.	UPON DISCOVERY OF ANY DISCREPANCIES BETWEEN DRAWINGS AND DEPICTING EXISTING CONDITIONS OR UPON DISCOVERY OF UNKNOWN CONDITIONS DETRIMENTAL TO THE COMPLETION OF THE WORK AS INDICATED IN THE DOCUMENTS, THE CONTRACTOR SHALL IMMEDIATELY NOTIFY ARCHITECT AND THE RESIDENT ENGINEER, IN WRITING, OF THE CONDITION IN QUESTION BEFORE PROCEEDING WITH WORK IN THAT AREA. SEE DETAIL 16AEB11.
3.	WHERE LAY-IN CEILING UNITS LESS THAN 6 INCHES WIDE OCCUR AT EDGES OF ROOM WITH 2X24 INCH PATTERN PROVIDE 24X48 INCH PANELS CUT TO EXTEND TO WALL ELIMINATING THE TEE NEAR THE WALL.
4.	THE PROPER LAYOUT OF THE RCP IS A COMBINATION OF ELECTRICAL & MECHANICAL PLANS AND THE CEILING FINISH CHOSEN. COORDINATION IS REQUIRED PRIOR TO INSTALLATION OF THE CEILING LIGHT FIXTURES, DIFFUSERS, ETC. COORDINATION/RESOLUTION TO CEILING CONFLICTS ARE TO BE APPROVED BY RESIDENT ENGINEER.
5.	SEE MECHANICAL AND ELECTRICAL SHEETS TO VERIFY SIZE, TYPE, NUMBER AND LOCATIONS OF FIXTURES.
6.	ALL LIGHTS TO BE CENTERED WITHIN 2X2 GRID (TYPICAL); ALL 2X2 GRIDS TO BE CENTERED WITHIN ROOM (TYPICAL).
7.	PROVIDE PAINTABLE ACCESS PANELS IN GYP BD CEILINGS AS REQ'D FOR ACCESS TO MECH & PLUMBING EQUIP. SEE MECH & PLUMBING FOR LOCATIONS.
8.	ALL SUSPENDED ACP AND GYPSUM BOARD CEILING HEIGHTS ARE AT 9'-0" AFF U.N.O. ALL GYPSUM BOARD SOFFITS ARE AT 7'-11" AFF U.N.O.
RCP KEY NOTES	
1A	PATIENT LIFT TRACK(VCI), 550# RE: SPECIALTY EQUIPMENT DRAWINGS (LIFTS), SEE DETAIL 13AEB11, 14AEB11, AND 16AEB11
1B	PATIENT LIFT TRACK(VCI), 770# RE: SPECIALTY EQUIPMENT DRAWINGS (LIFTS), SEE DETAIL 13AEB11, 14AEB11, AND 16AEB11
2	PRIVACY CURTAIN & TRACK
3	SHOWER CURTAIN & ROD
4	PROVIDE STEEL SUPPORT ABOVE SUSPENDED CEILING FOR CEILING MOUNTED TOILET PARTITIONS, SEE DETAIL 15AEB11
5	CEILING TRACK FOR DENTAL LIGHT
6	PROVIDE REINFORCED LENGTHS OF CEILING TRACKS AS REQUIRED TO ALLOW FOR REMOVAL OF 6' X 6' AREA OF ACT FOR ACCESS/USE OF THE ATTIC HATCH. SEE 11AE110.

CONFORMED SET
FOR CONSTRUCTION

			CONSULTANT  623 26th Avenue Rock Island, IL 61201 T: 309.788.0673 F: 309.786.5967		ARCHITECT/ENGINEER OF RECORD THOMAS OLESAC, ARCHITECT MS Lic # 5505 1050 HOYT AVE WEST ST PAUL, MN 55117 952-451-0460		STAMP  05.12.2025		Office of Construction and Facilities Management  U.S. Department of Veterans Affairs		Drawing Title 4TH FLOOR REFLECTED CEILING PLAN Approved:		Phase CONSTRUCTION DOCUMENTS FULLY SPRINKLERED		Project Title RENOVATE BUILDING 1 Location BILOXI, MISSISSIPPI Issue Date 05/12/2025 Checked LA Drawn CD,PC		Project Number 520-317X Building Number 1 Drawing Number AE112 Dwg. 76 of 239	
<table><tr><th>NO.</th><th>REVISIONS</th><th>DATE</th></tr><tr><td> </td><td> </td><td> </td></tr><tr><td> </td><td> </td><td> </td></tr><tr><td> </</td></tr></table>			NO.	REVISIONS	DATE	</
NO.	REVISIONS	DATE	
</	

C:\Users\pjd\Documents\15950 - VAIC-Bldg Building 1_R22 - Central mode_Yunyoung.nrt
5/14/2025 7:01:16 AM
VA FORM 08 - 6231

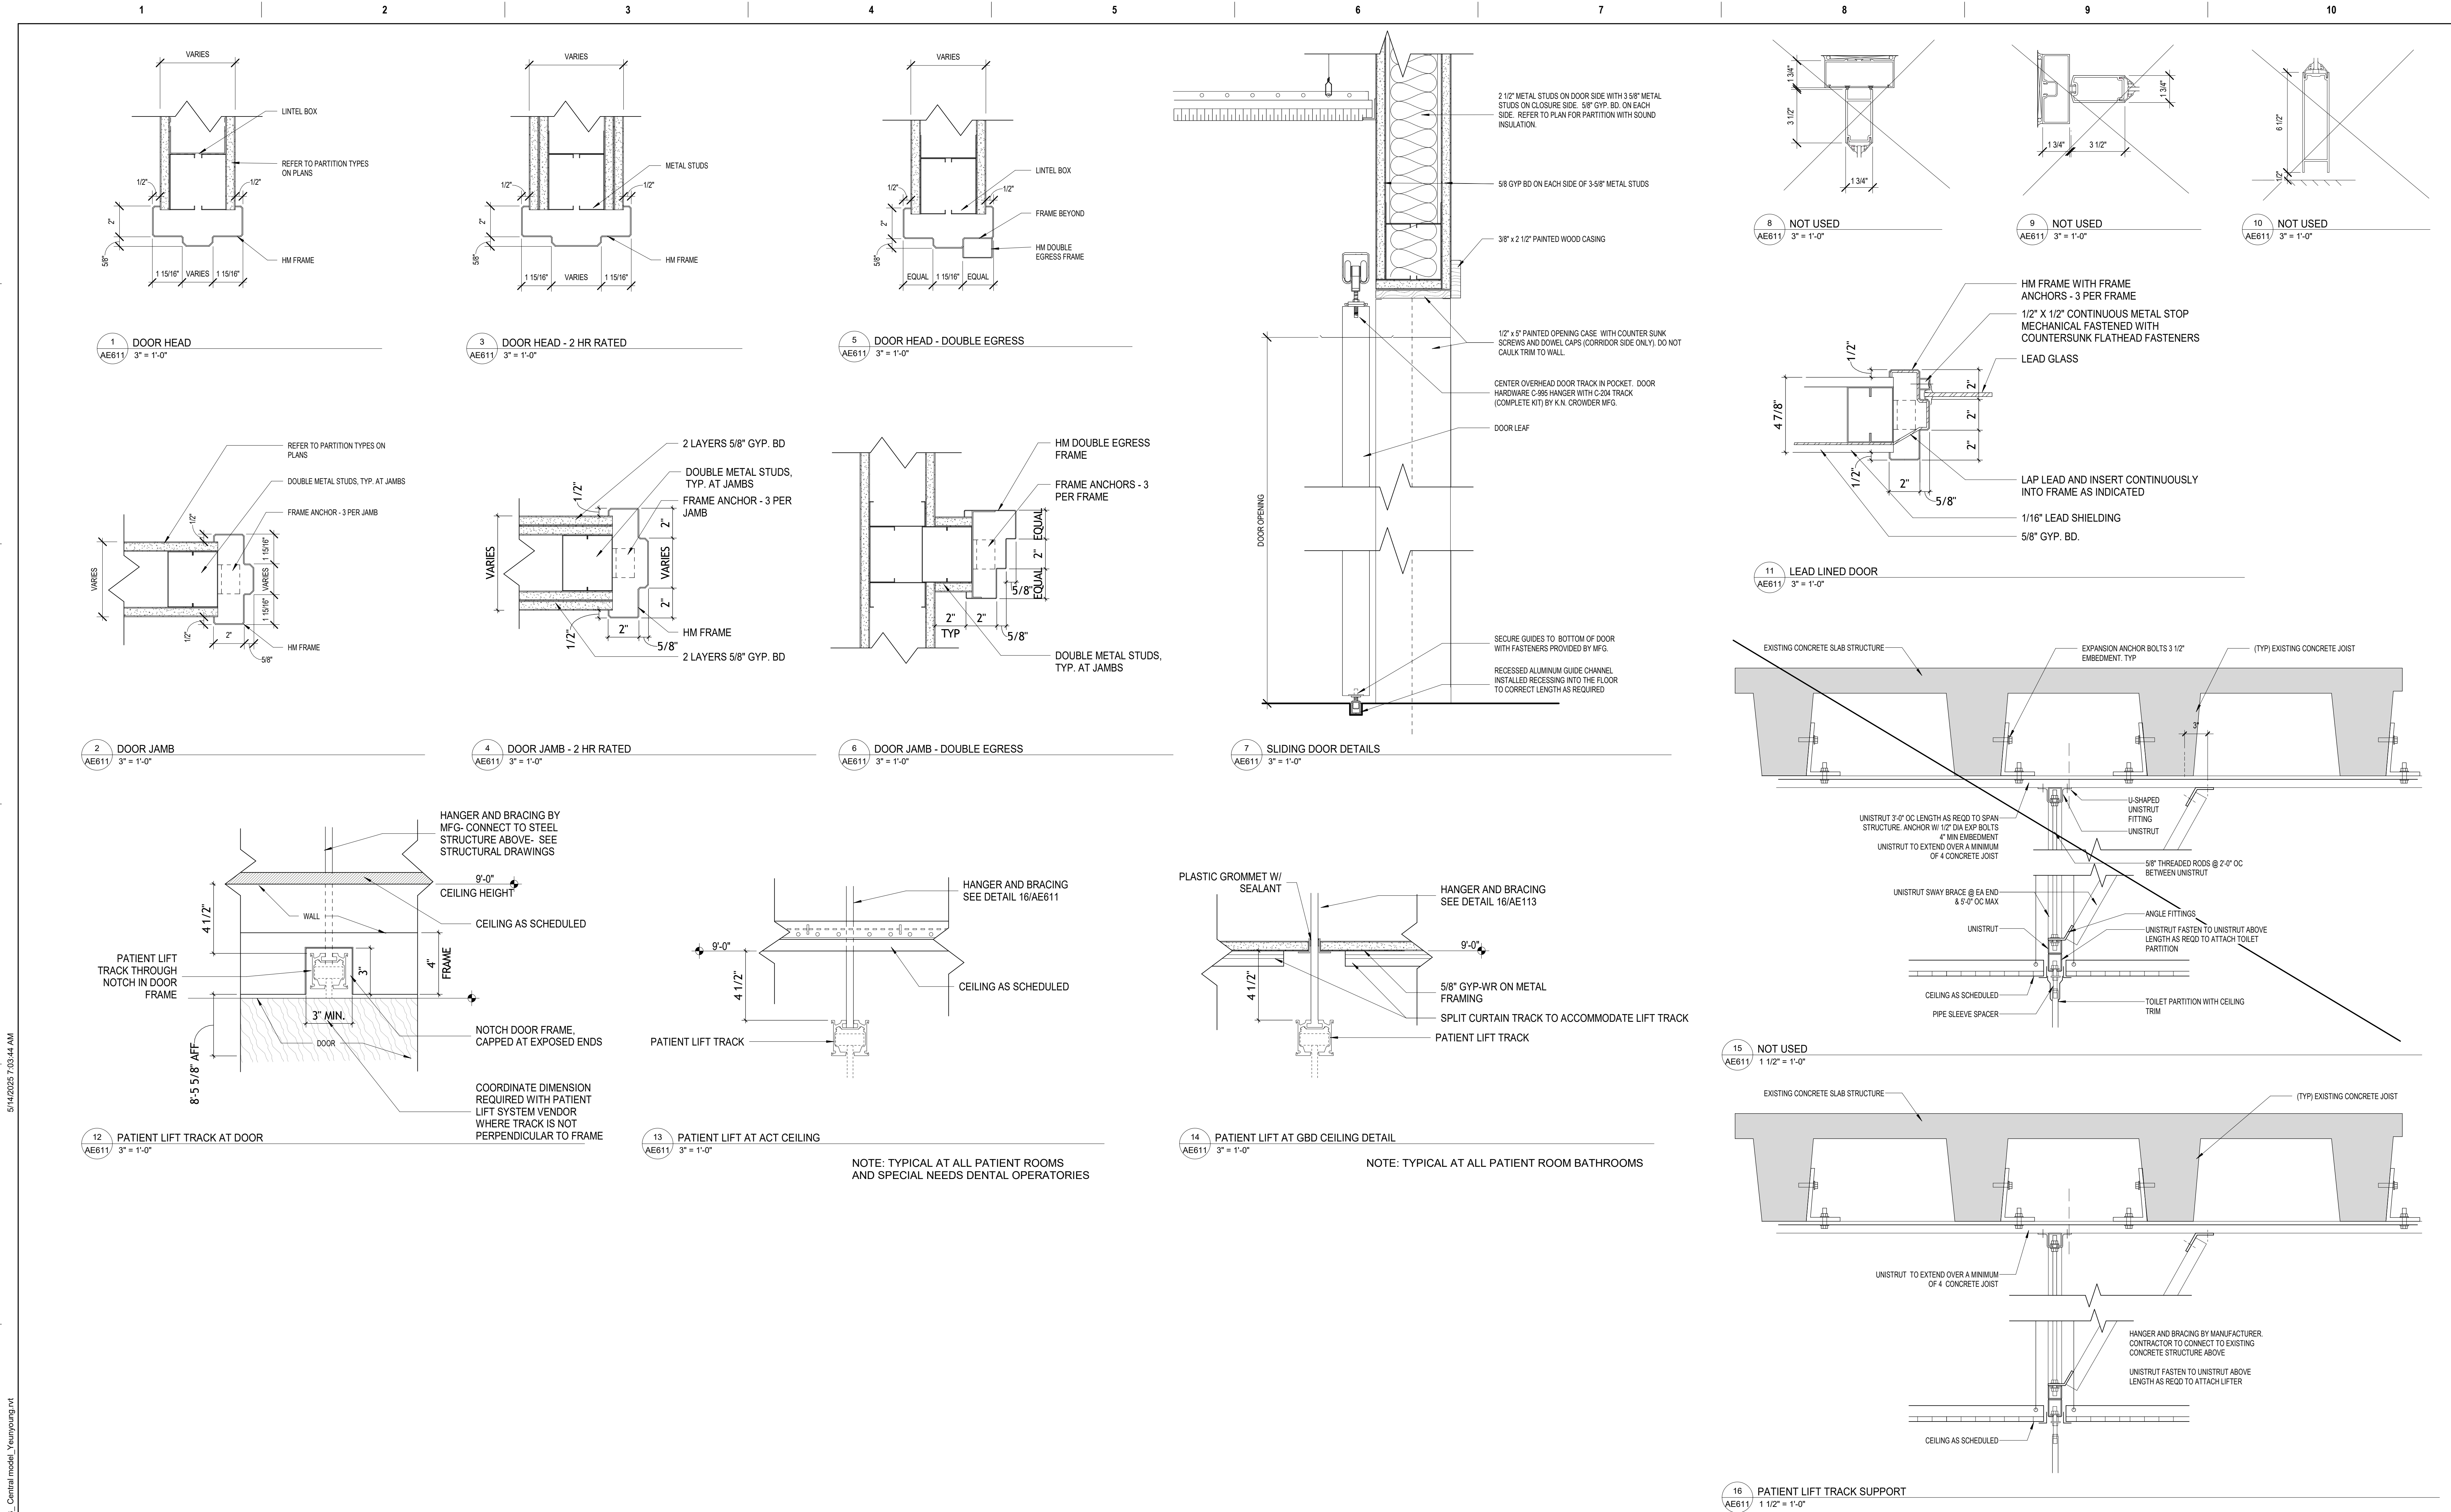

CONFORMED SET
FOR CONSTRUCTION

NO.	REVISIONS	DATE

CONSULTANT



623 26th Avenue
Rock Island, IL 61201
T: 309.788.9673
F: 309.786.5967

ARCHITECT/ENGINEER OF RECORD

THOMAS OLESAC, ARCHITECT

MS Lic # 5505

1050 HOYT AVE WEST ST PAUL, MN 55117
952-451-0460

STAMP



Office of
Construction
and Facilities
Management

 U.S. Department of
Veterans Affairs

Drawing Title

DOOR DETAILS

Approved:

Phase

CONSTRUCTION
DOCUMENTS

FULLY SPRINKLERED

Project Title

RENOVATE BUILDING 1

Location

BILOXI, MISSISSIPPI

Issue Date

05/12/2025

Checked

LA

Drawn

PC

Project Number

520-317X


Building Number

1

Drawing Number

AE611


Dwg. 109 of 239

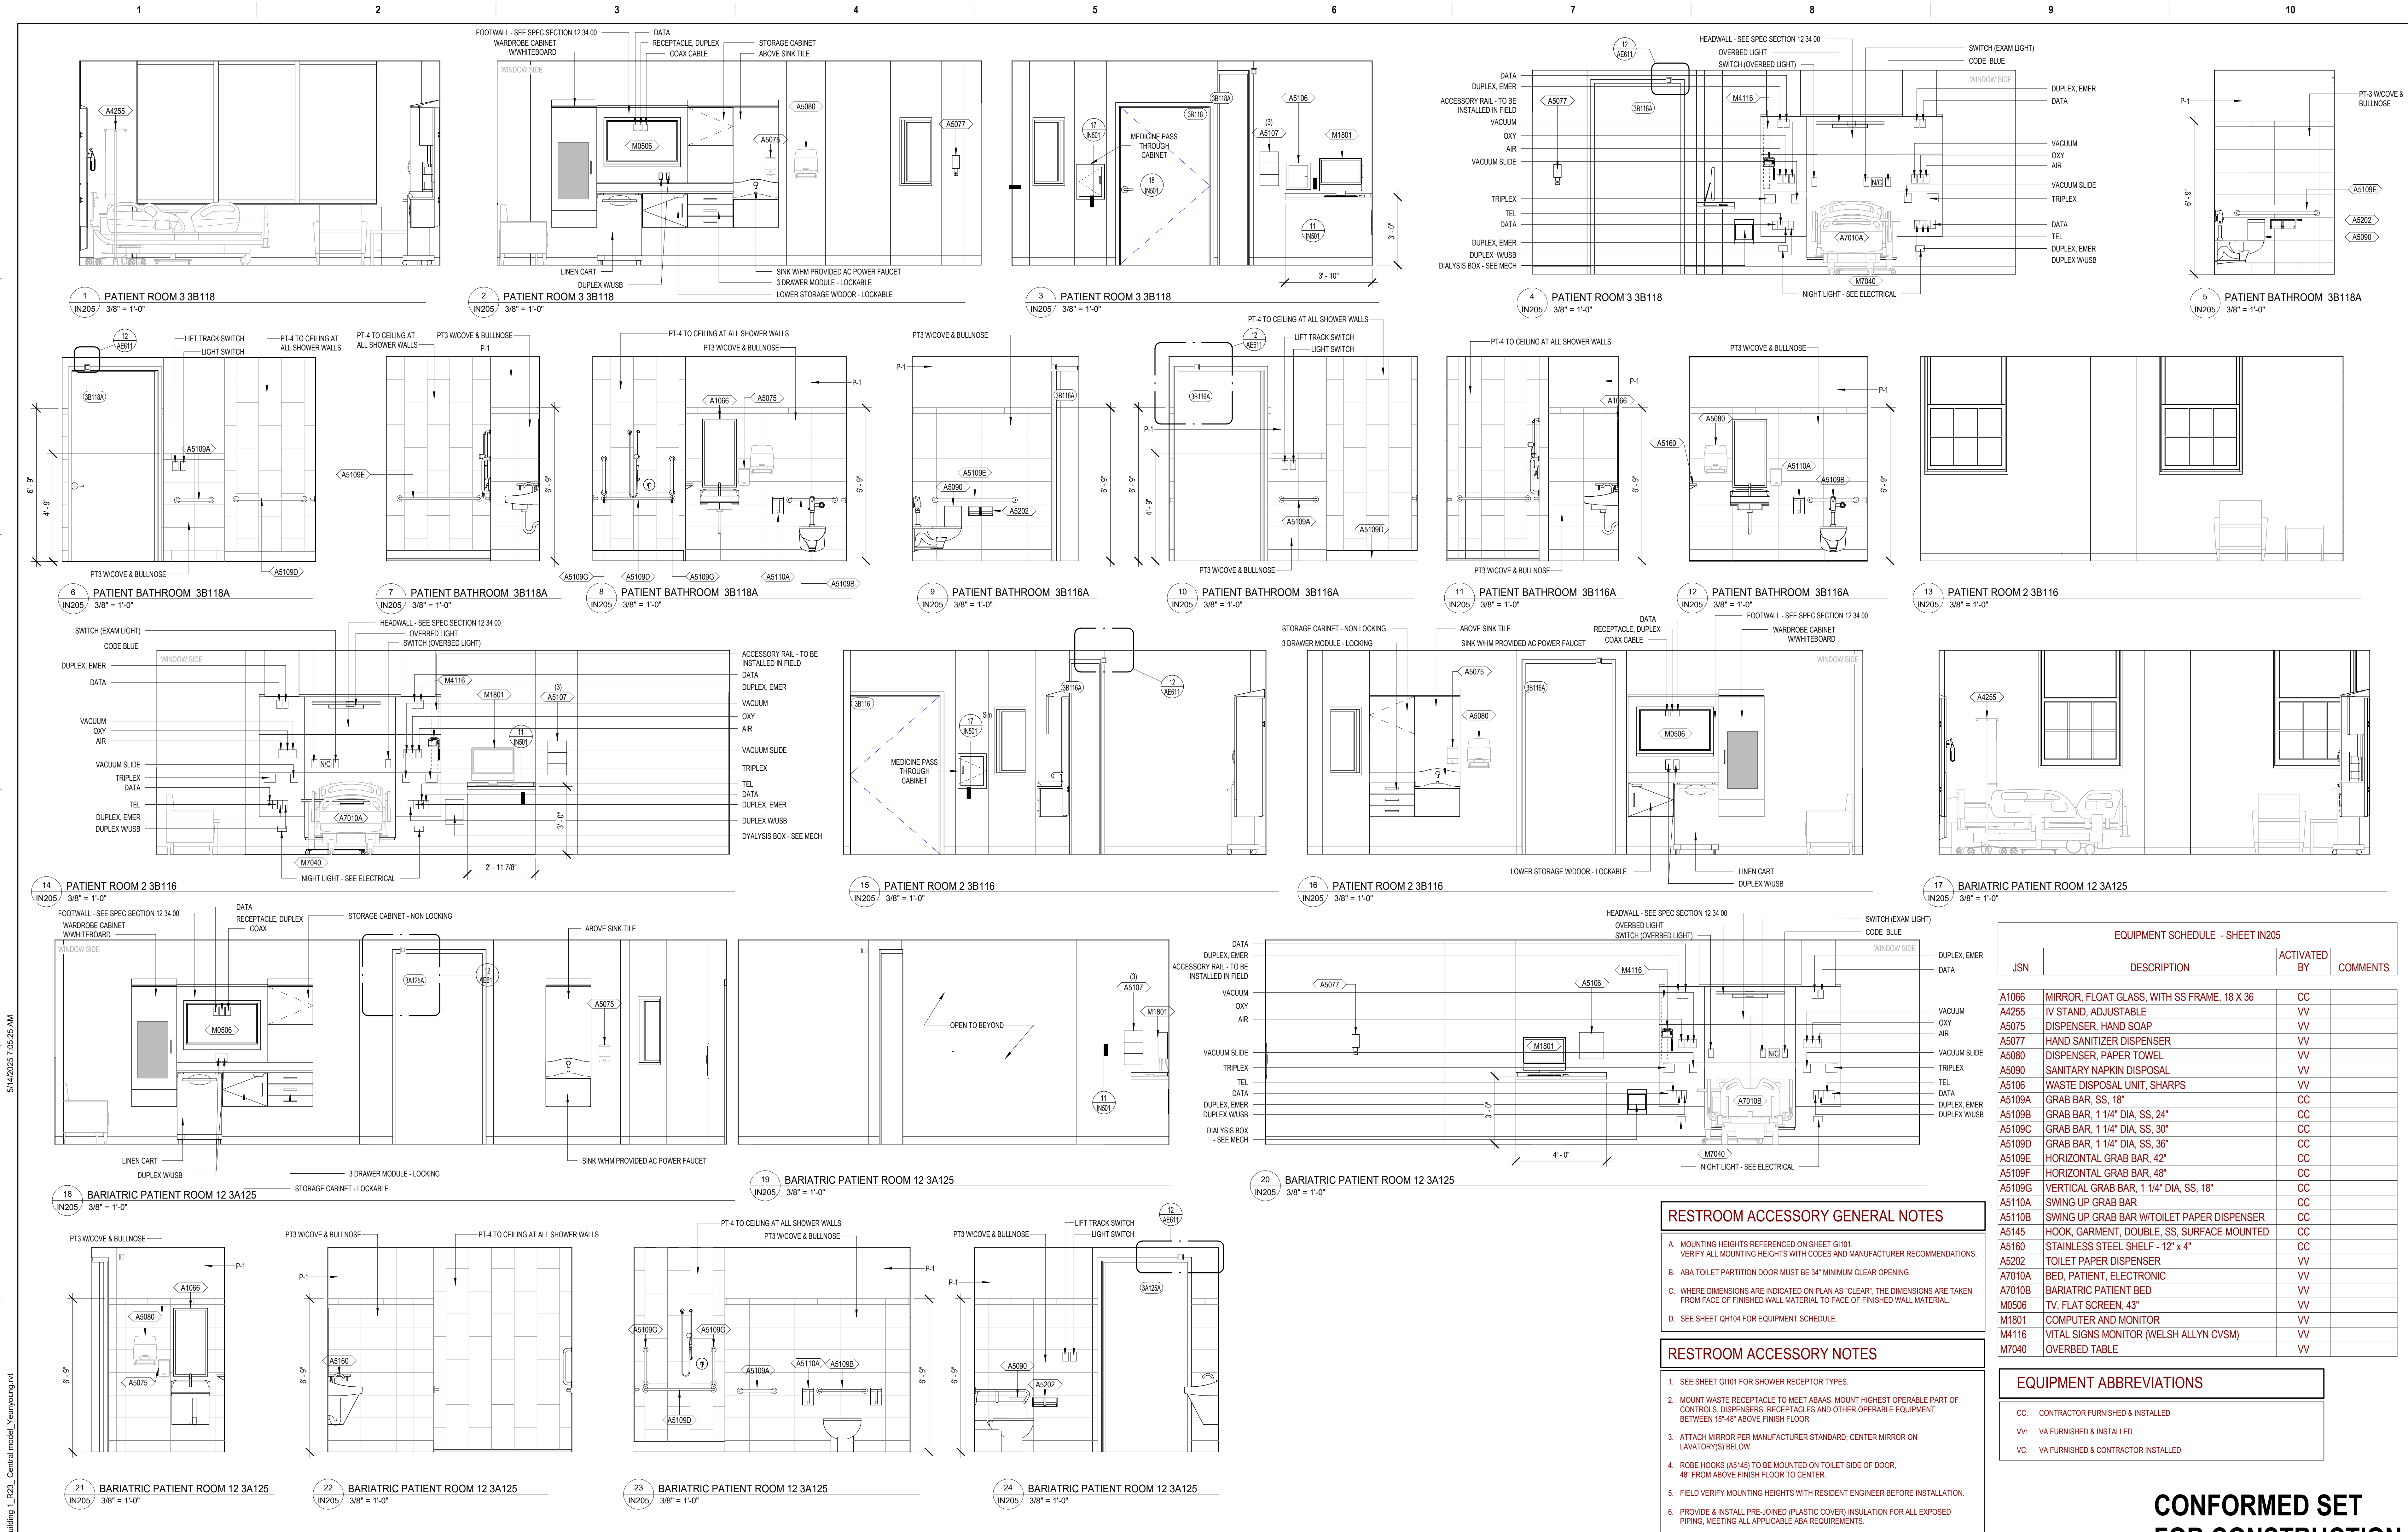

CONFORMED SET
FOR CONSTRUCTION

CONSULTANT		ARCHITECT/ENGINEER OF RECORD		STAMP		Office of Construction and Facilities Management		Drawing Title		Phase		Project Title		Project Number	
IMEG		THOMAS OLESACK, ARCHITECT		THOMAS OLESACK		Office of Construction and Facilities Management		INTERIOR ELEVATIONS		CONSTRUCTION DOCUMENTS		RENOVATE BUILDING 1		520-317X	
623 26th Avenue Rock Island, IL 61201 T: 309.788.0673 F: 309.786.5967		MS Lic # 5505		05.12.2025		VA		Approved:		FULLY SPRINKLERED		BLOXI, MISSISSIPPI		Building Number 1	
NO. REVISIONS DATE		1050 HOYT AVE WEST ST PAUL, MN 55117 952-451-0460				U.S. Department of Veterans Affairs						Issue Date 05/12/2025		Drawing Number IN205	
												Checked LA		Dwg. 126 of 239	
												Drawn MP, PC, JT			

1	2	3	4	5	6	7	8	9	10
---	---	---	---	---	---	---	---	---	----

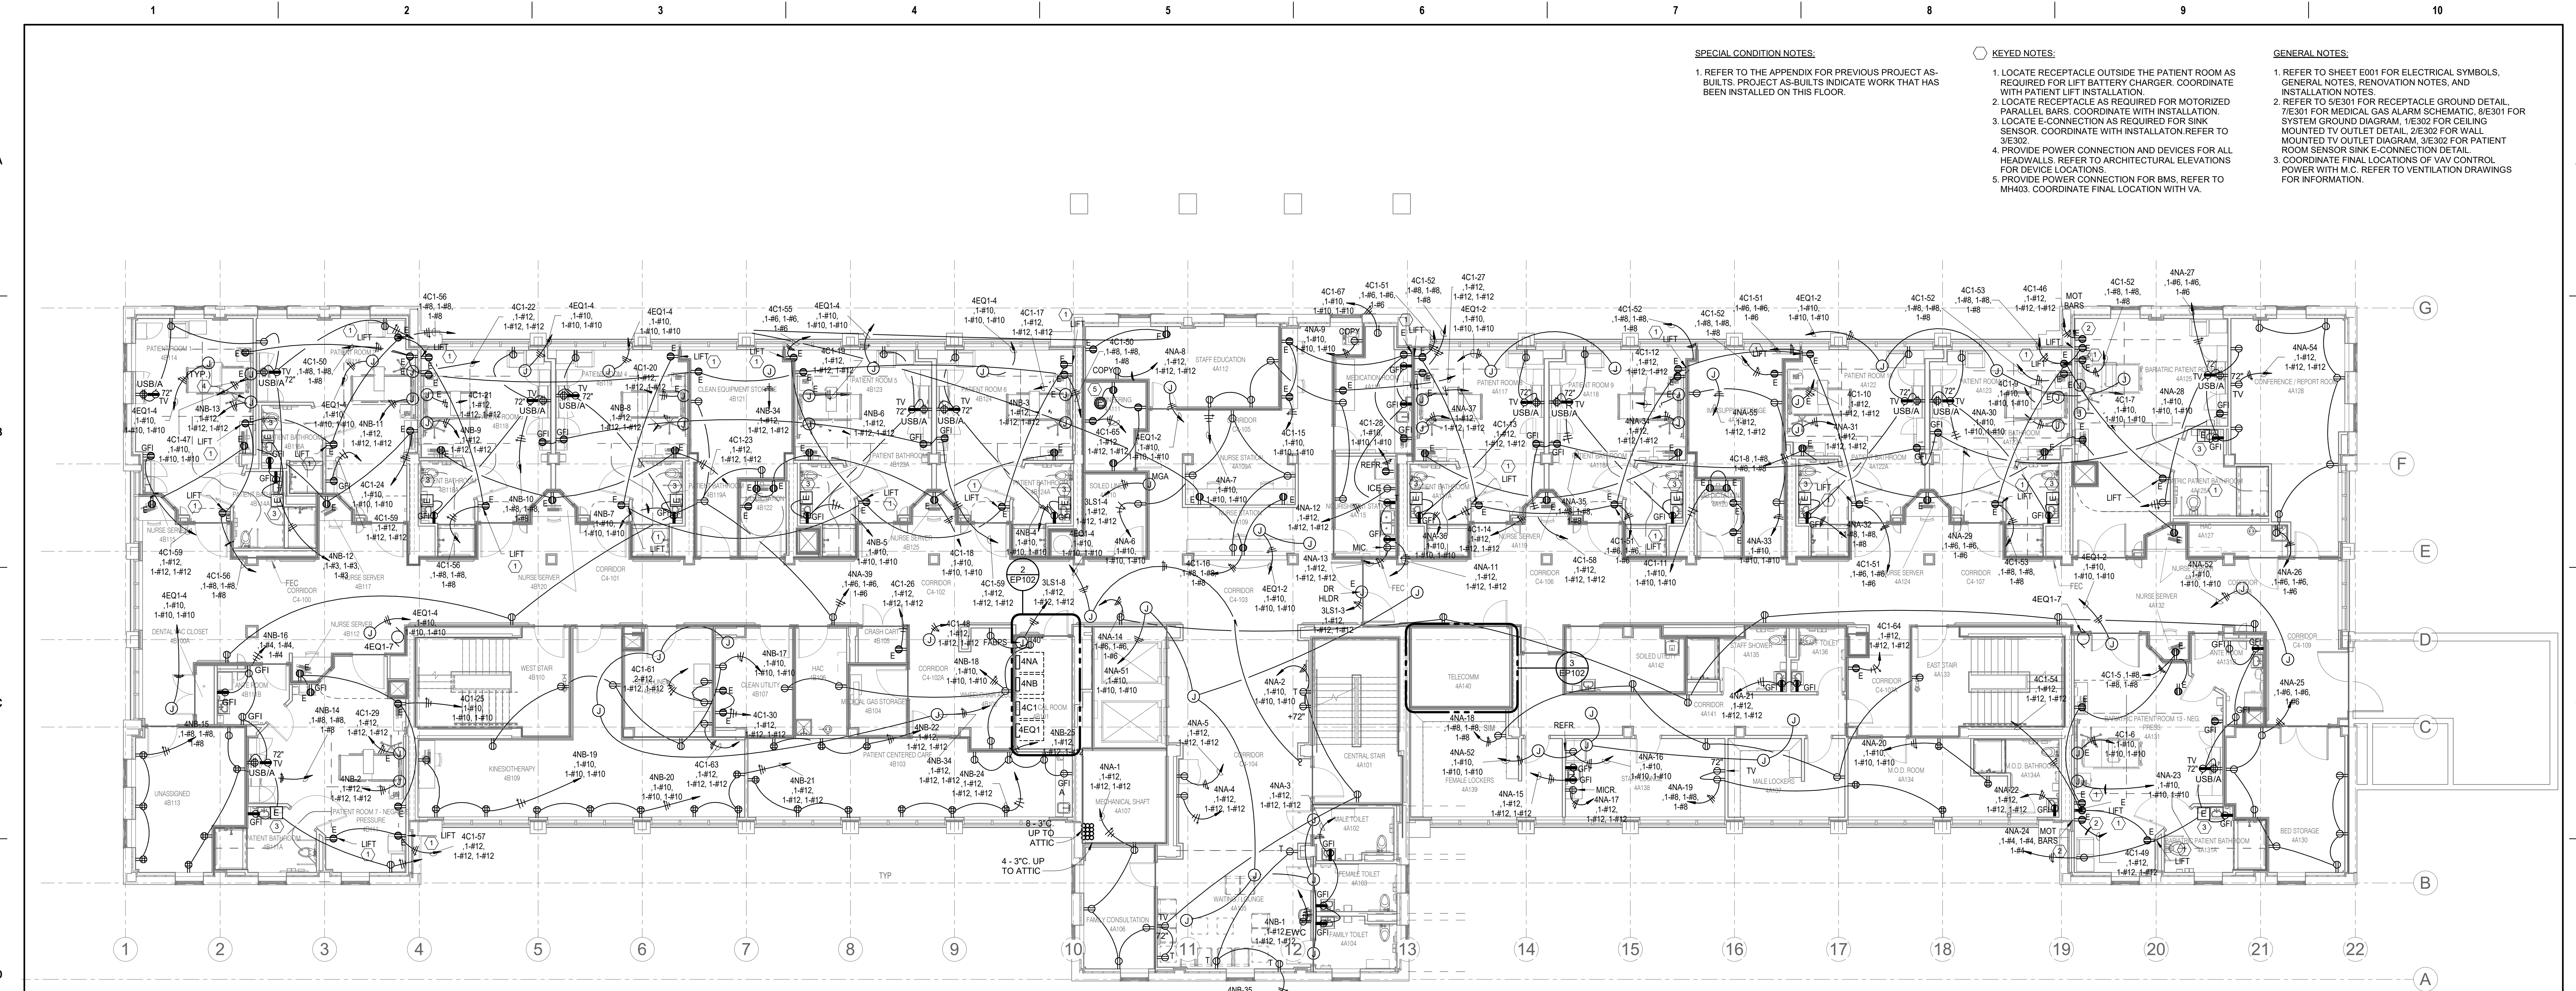

SPECIAL CONDITION NOTES:

1. REFER TO THE APPENDIX FOR PREVIOUS PROJECT AS-BUILTS. PROJECT AS-BUILTS INDICATE WORK THAT HAS BEEN INSTALLED ON THIS FLOOR.

KEYED NOTES:


1. LOCATE RECEPTACLE OUTSIDE THE PATIENT ROOM AS REQUIRED FOR LIFT BATTERY CHARGER. COORDINATE WITH PATIENT LIFT INSTALLATION.
2. LOCATE RECEPTACLE AS REQUIRED FOR MOTORIZED PARALLEL BARS. COORDINATE WITH INSTALLATION.
3. LOCATE E-CONNECTION AS REQUIRED FOR SINK SENSOR. COORDINATE WITH INSTALLATION. REFER TO 3/E302.
4. PROVIDE POWER CONNECTION AND DEVICES FOR ALL HEADWALLS. REFER TO ARCHITECTURAL ELEVATIONS FOR DEVICE LOCATIONS.
5. PROVIDE POWER CONNECTION FOR BMS. REFER TO MH403. COORDINATE FINAL LOCATION WITH VA.

GENERAL NOTES:


1. REFER TO SHEET E001 FOR ELECTRICAL SYMBOLS, GENERAL NOTES, RENOVATION NOTES, AND INSTALLATION NOTES.
2. REFER TO G6301 FOR RECEPTACLE GROUND DETAIL, 7/E301 FOR MEDICAL GAS ALARM SCHEMATIC, 8/E301 FOR SYSTEM GROUND DIAGRAM, 1/E302 FOR CEILING MOUNTED TV OUTLET DETAIL, 2/E302 FOR WALL MOUNTED TV OUTLET DETAIL, 3/E302 FOR PATIENT ROOM SENSOR SINK E-CONNECTION DETAIL.
3. COORDINATE FINAL LOCATIONS OF VAV CONTROL POWER WITH M.C. REFER TO VENTILATION DRAWINGS FOR INFORMATION.

NOTE: SEE SHEET "IN102" FOR INTERIOR ELEVATION REFERENCE

1
4TH FLOOR - POWER
1/8" = 1'-0"

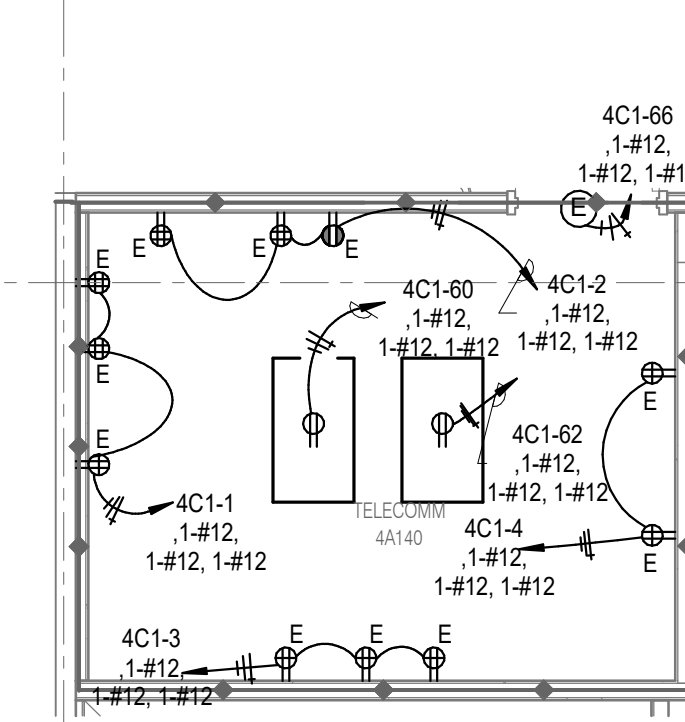

3
LARGE SCALE TELECOMM ROOM 4A139 PLAN - POWER
1/4" = 1'-0"

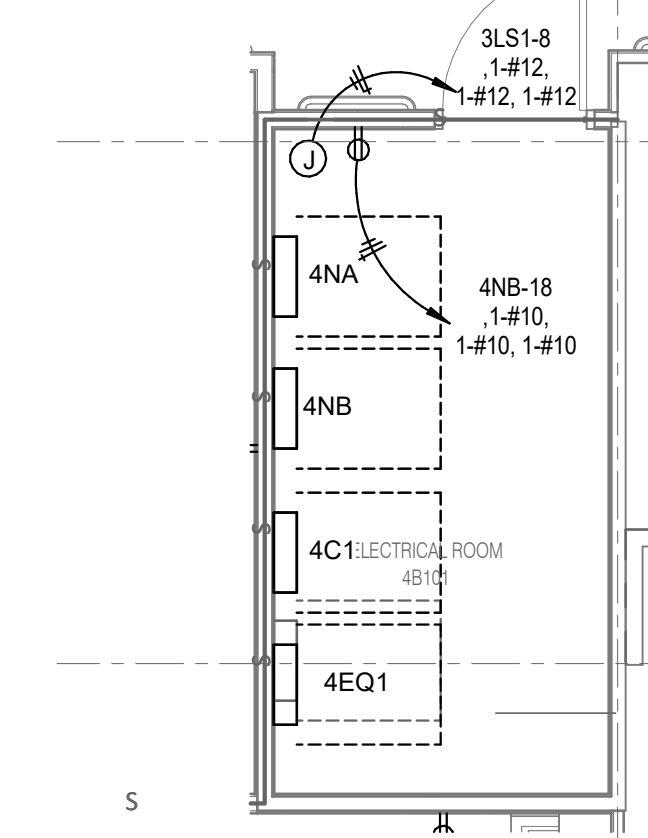

2
LARGE SCALE ELECTRICAL ROOM 1-4B101 - POWER
1/4" = 1'-0"

**CONFORMED SET
FOR CONSTRUCTION**

	CONSULTANT		ARCHITECT/ENGINEER OF RECORD		STAMP 	Office of Construction and Facilities Management	Drawing Title 4TH FLOOR - POWER	Phase CONSTRUCTION DOCUMENTS	Project Title RENOVATE BUILDING 1	Project Number 520-317X	
	IMEG		ANDERSON							Building Number 1	
	623 26th Avenue Rock Island, IL 61201 T: 309.788.0673 F: 309.786.5967		13605 1st Ave. N. #100 Plymouth, MN 55441 P 763.412.4000 F 763.412.4090 ae-mn.com Anderson Engineering of Minnesota, LLC Proj #							Drawing Number EP102	
	Revisions:		Date:							Dwg. 214 of 239	
						VA U.S. Department of Veterans Affairs	Approved:	Fully Sprinklered	Location BILOXI, MISSISSIPPI		
				Issue Date 05/12/2025					Checked IMEG	Drawn STEWIE	


A
B
C
D
E
F

5/9/2025 3:05:14 PM

C:\Revit\Local\Bldg1\40317_BLDG1_Electrical\CD\Jaron.C.Meyer.rvt


VA FORM 08 - 6231

- SPECIAL CONDITION NOTES:**
1. REFER TO THE APPENDIX FOR PREVIOUS PROJECT AS-BUILTS. PROJECT AS-BUILTS INDICATE WORK THAT HAS BEEN INSTALLED ON THIS FLOOR.
- KEYED NOTES:**
1. INSTALL JBOX FOR CUBICLE CIRCUITS ABOVE CEILING. ROUTE CONDUIT AND WIRE DOWN COLUMNS. CONFIRM WHIP WITH FURNITURE INSTALLER. CONCEALED COORDINATE TERMINATION OF CIRCUITRY WITH THE CUBICLE MANUFACTURER.
 2. REFER TO ARCHITECTURAL ELEVATIONS FOR DEVICE LOCATIONS. COORDINATE HEIGHT WITH BACKSPLASH. MIN. 6" ABOVE BACKSPLASH. REFER TO ARCHITECTURAL ELEVATIONS.
 3. CONNECTION FOR EXAM LIGHT AND MONITOR. LOCATE ABOVE CEILING ACCESSIBLE. EXAM LIGHT FURNISHED BY OTHERS. TO BE INSTALLED BY ELECTRICAL CONTRACTOR.
 4. PROVIDE POWER CONNECTION FOR HOOD INCLUDING INTERNAL LIGHTING AND RECEPTACLES. COORDINATE REQUIREMENTS WITH INSTALLER.
 5. SWITCH TO OPERATE X-RAY WITH CONDUIT PATHWAY TO X-RAY CONNECTION.
 6. PROVIDE GROUND WIRE AND CONNECTION TO FLAMMABLE CABINET. UTILIZE NEAREST ELECTRICAL PANEL GROUND BUS FOR CONNECTION TO BUILDING GROUNDING SYSTEM.
 7. PROVIDE POWER CONNECTION FOR BMS. REFER TO MH403. COORDINATE FINAL LOCATION WITH VA.
- GENERAL NOTES:**
1. REFER TO SHEET E001 FOR ELECTRICAL SYMBOLS, GENERAL NOTES, RENOVATION NOTES, AND INSTALLATION NOTES.
 2. REFER TO S6301 FOR RECEPTACLE GROUND DETAIL, 7/8301 FOR MEDICAL GAS ALARM SCHEMATIC, 8/301 FOR SYSTEM GROUND DETAIL, 1/302 FOR CEILING MOUNTED TV OUTLET DETAIL, 2/302 FOR WALL MOUNTED TV OUTLET DETAIL, 4/301 FOR FLOOR SLAB PENETRATION DETAIL.
 3. COORDINATE FINAL LOCATIONS OF VAV CONTROLS POWER WITH M.C. REFER TO VENTILATION DRAWINGS FOR INFORMATION.
 4. PROVIDE ELECTRICAL CONNECTIONS TO DENTAL FURNITURE DEVICES. COORDINATE INSTALLATION WITH FURNITURE INSTALLER.
 5. COORDINATE ALL DEVICE LOCATIONS WITH ARCHITECTURAL ELEVATIONS FOR THE DENTAL LAB AND DENTAL OPERATORY.
 6. COORDINATE FLOOR BOX LOCATIONS IN DENTAL LAB WITH EQUIPMENT AND DENTAL CHAIRS. VERIFY LOCATIONS WITH VA PRIOR TO INSTALLATION.

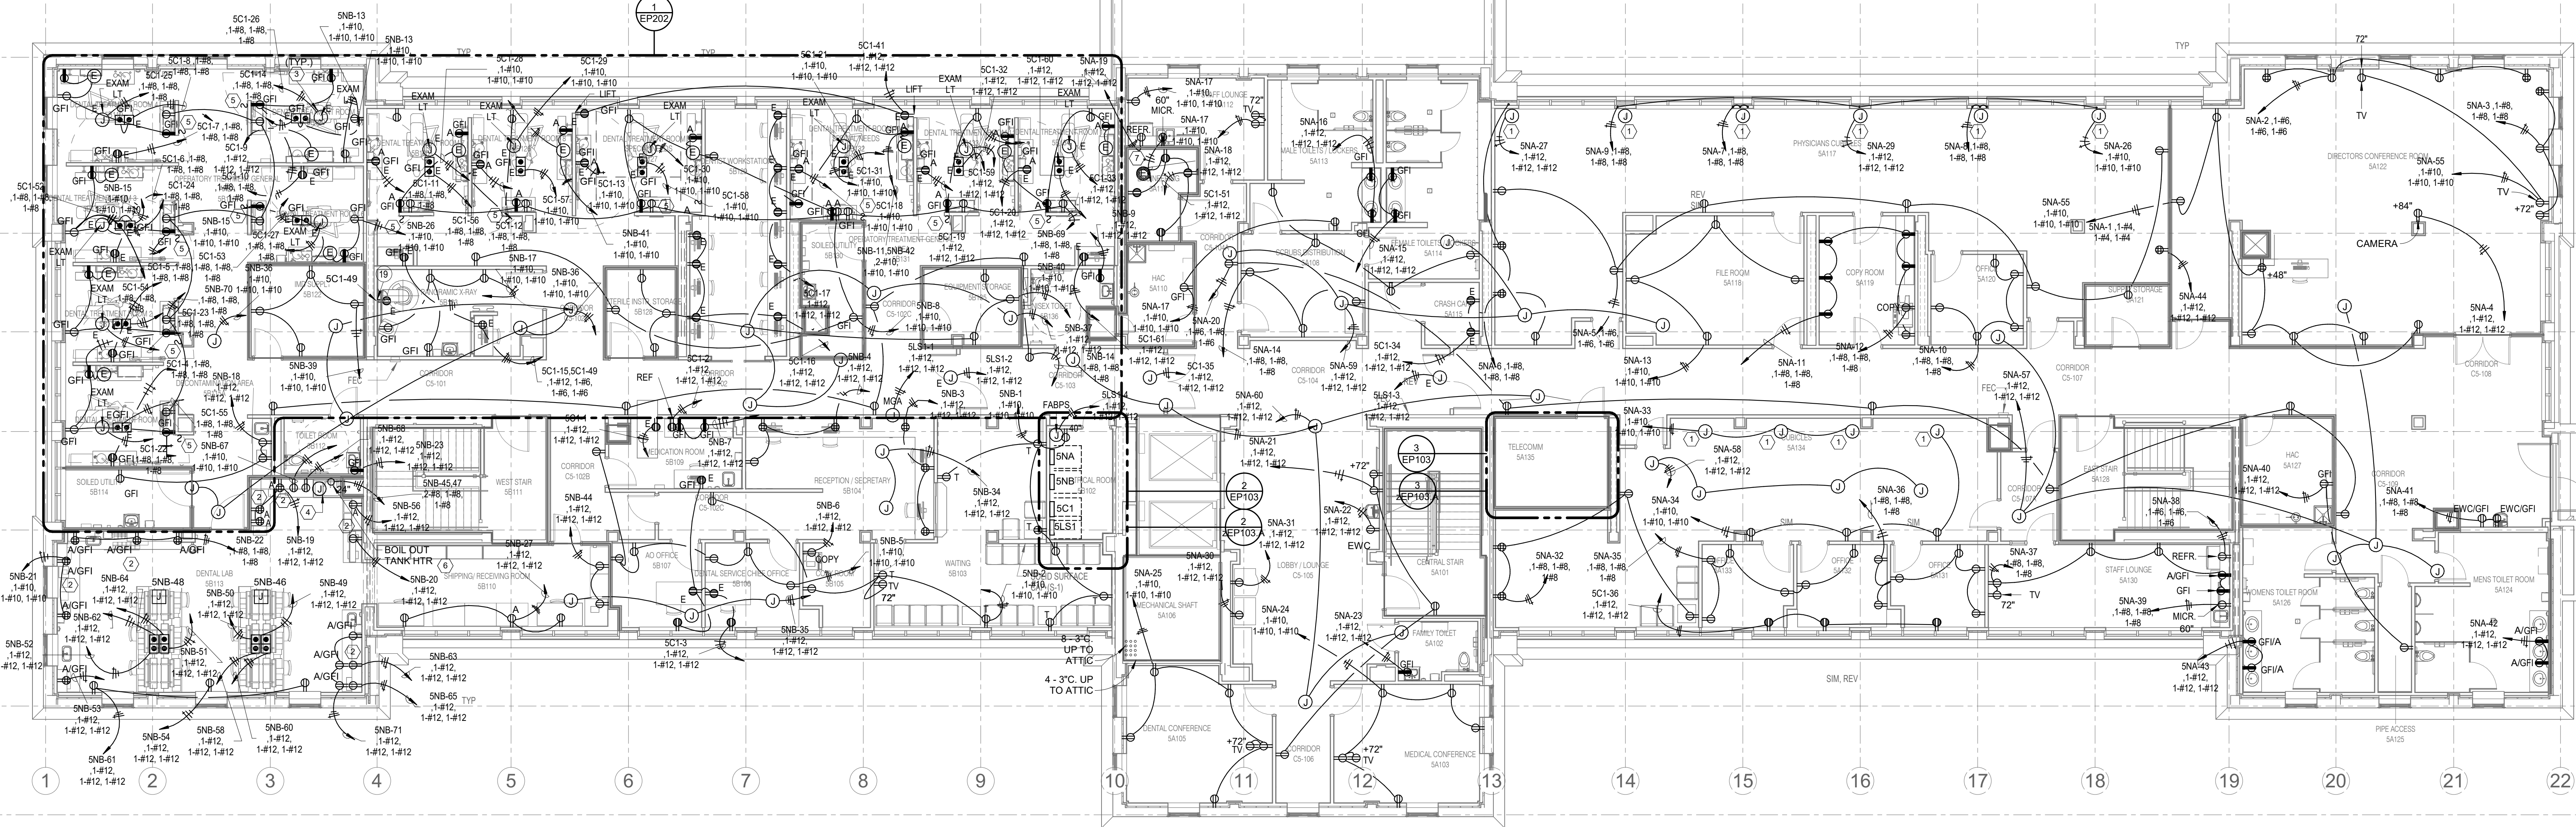


NOTE: SEE SHEET "IN103" FOR INTERIOR ELEVATION REFERENCE

1
5TH FLOOR - POWER
1/8" = 1'-0"

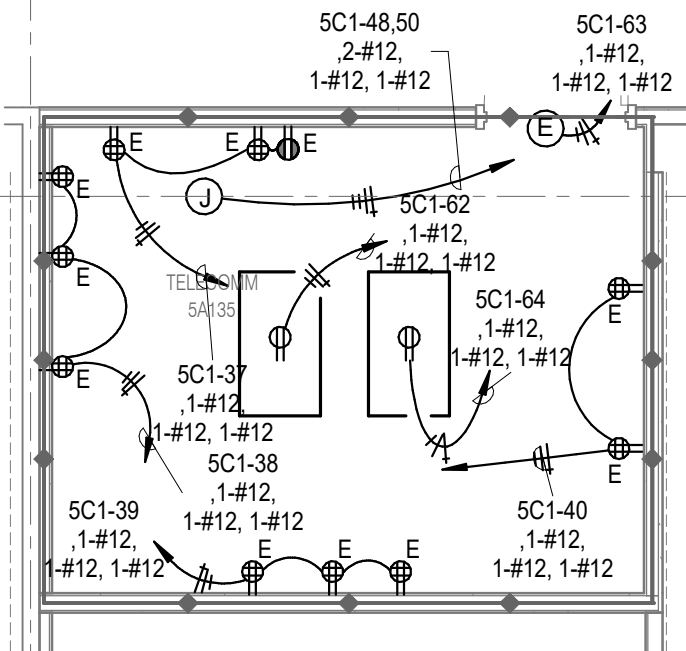

3
LARGE SCALE TELECOM ROOM SA135 - POWER
1/4" = 1'-0"

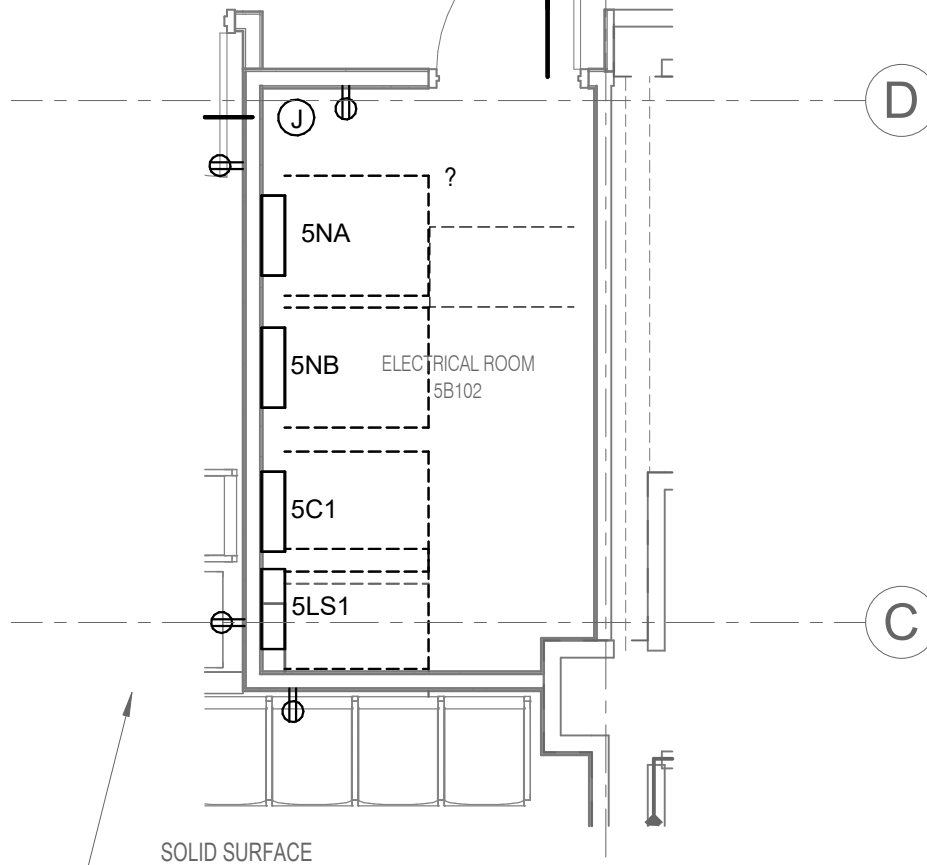

2
LARGE SCALE ELECTRICAL ROOM 1-5B102 - POWER
1/4" = 1'-0"

CONFORMED SET
FOR CONSTRUCTION

Revisions:	
------------	--	--	


05-12-2025
Exp 12-31-2025

GENERAL NOTES:

1. REFER TO SHEET E001 FOR ELECTRICAL SYMBOLS, GENERAL NOTES, RENOVATION NOTES, AND INSTALLATION NOTES.

KEYED NOTES:

1. PROVIDE A CONDUIT FROM EXAM LIGHT TO TROUGH UNDERNEATH CHAIR FOR EXAM LIGHT CONTROL CABLE.

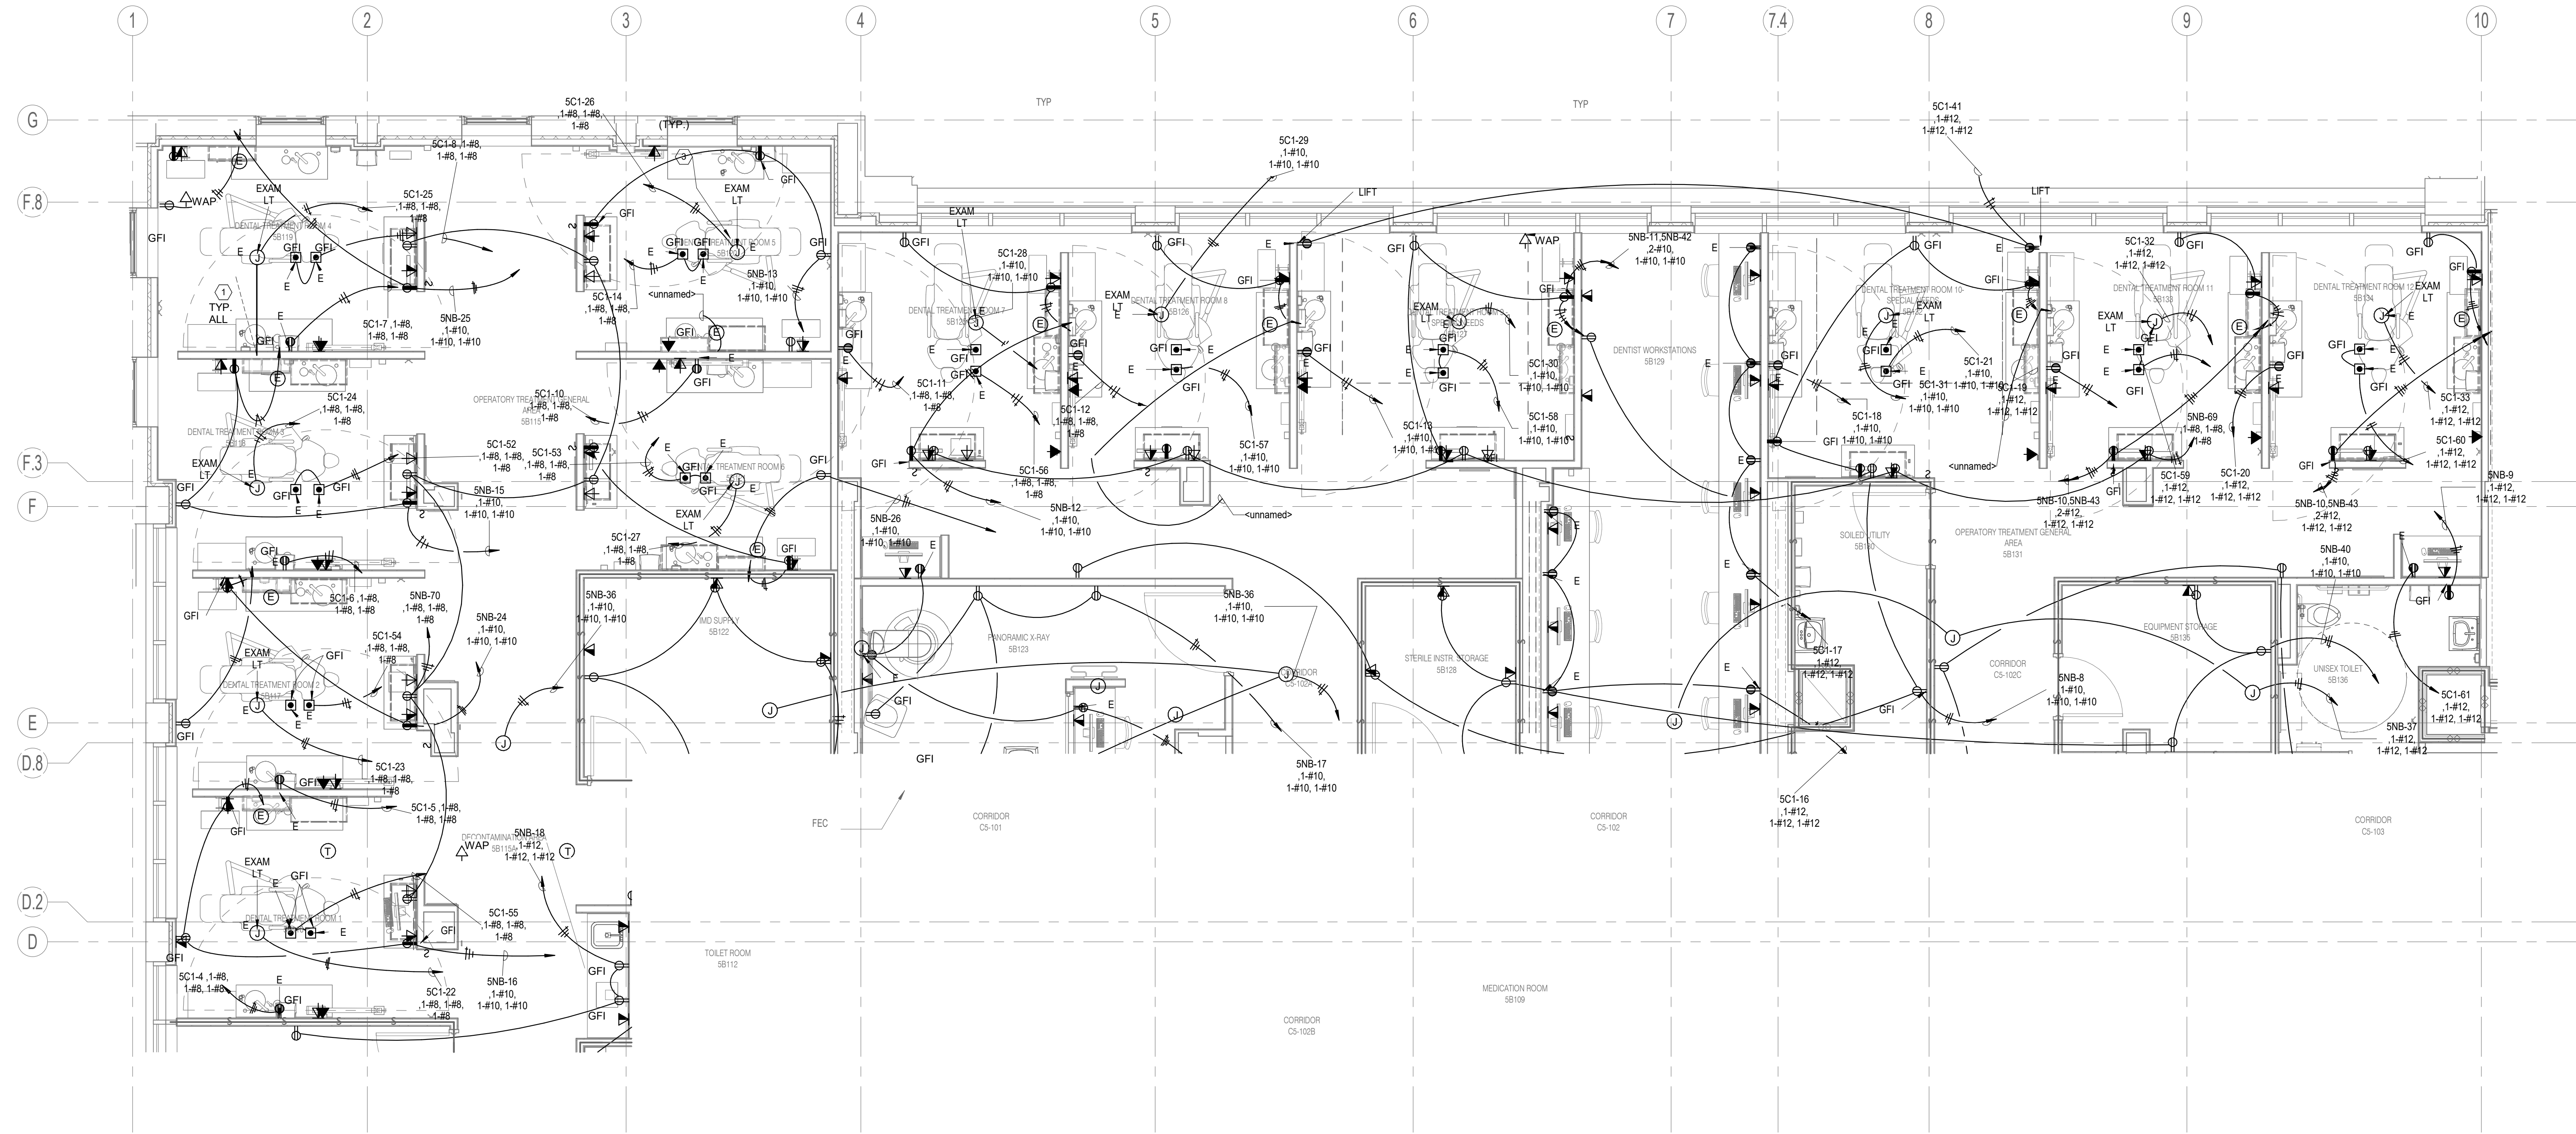

1 LARGE SCALE DENTAL TREATMENT PLAN - POWER AND TELECOM
1/4" = 1'-0"

CONFORMED SET
FOR CONSTRUCTION

Revisions:	Date:

CONSULTANT

IMEG

623 26th Avenue
Rock Island, IL 61201
T: 309.788.0673
F: 309.786.5967

ARCHITECT/ENGINEER OF RECORD

ANDERSON

13605 1st Ave. N. #100 Plymouth, MN 55441
P 763.412.4000 | F 763.412.4090 | ae-mn.com
Anderson Engineering of Minnesota, LLC | Proj #

STAMP

PAUL WARD
LICENSED PROFESSIONAL
ENGINEER
29752
STATE OF MISSISSIPPI

Office of
Construction
and Facilities
Management

VA U.S. Department
of Veterans
Affairs

Drawing Title
ENLARGED PLANS - POWER AND
TELECOM

Approved:

Phase
CONSTRUCTION
DOCUMENTS

FULLY SPRINKLERED

Project Title RENOVATE BUILDING 1	Project Number 520-317X
Location BILOXI, MISSISSIPPI	Building Number 1
Issue Date 05/12/2025	Checked IMEG
Drawn STEWIE	Drawing Number EP202
Dwg. 218 of 239	

5/9/2025 3:05:31 PM

C:\Revit Local Files\ICT 140317_BLDG 1_Electrical CDS_Jason C Meyer.rvt

05-12-2025
Exp 12-31-2025

NOTES:

1. ALL LINEAR FIXTURES SHALL BE MINIMUM 48,000 HOURS AVERAGE LIFE.
2. SUFFIX "D" BESIDE FIXTURE ON PLANS NOTES TO SUPPLY A 0-10V DIMMING DRIVER FOR THE FIXTURE.
3. COORDINATE WITH VA FOR EQUIPMENT PURCHASED AND ONSITE.

NOTES:
1. ULTRASONIC SENSORS SHOULD BE KEPT MINIMUM 6" AWAY FROM HVAC SUPPLY REGISTERS.
2. * = SEE SPECS FOR DEVICE COLOR.

REMARKS:

- 1. CIRCUIT TO INCLUDE ONE (1) GREEN GROUNDING CONDUCTOR SIZED PER BRANCH CIRCUIT SIZE UNLESS SHOWN TO BE SIZED DIFFERENTLY. ALL CONDUCTORS TYPE THW.
- 2. DUAL ELEMENT TYPE FUSE AND SWITCH OF PROPER VOLTAGE. IF FUSE SIZE NOT SHOWN, UNIT TO BE UNFUSED.
- 3. FINAL CONNECTION USING LIQUID TIGHT FLEXIBLE CONDUIT.
- 4. FINAL CONNECTION USING FLEXIBLE CONDUIT.
- 5. MOUNT ABOVE CEILING.
- 6. WALL MOUNTED.
- 7. VERIFY ALL ELECTRICAL REQUIREMENTS WITH MANUFACTURER'S SHOP DRAWINGS
- 8. DISCONNECT SWITCH INTEGRAL WITH UNIT.
- 9. EACH FAN TO BE PROTECTED SEPARATELY.
- 10. PROVIDE LABELS IN ACCORDANCE WITH NEC TO INSTALL THIS DEVICE.
- 11. MOUNT DISCONNECT ON SIDE OF UNIT.
- 12. VSM/VARIABLE FREQUENCY DRIVE (SCHEDULE AND SPECIFICATION SECTION 26 29 11) FOR MORE INFORMATION. SEE PROJECT MANUAL FOR MANUAL MOTOR STARTER FOR EACH FAN MOTOR IN THE SUPPLY/RETURN AIRWAY FOR OVERLOAD PROTECTION.

STARTER TYPE:	REMARKS:
PWM - PULSE WIDTH MODULATED	SA - STANDARD ACCESSORIES
18PWM - 12 PULSE PWM	IS - ISOLATION TRANSFORMER
18PWM - 18 PULSE PWM	"SH" - SKIP FREQUENCY CAPABILITY
LINE DISCONNECT	RSS - REMOTE START-STOP
DS - DISCONNECT SWITCH	RDR - REMOTE DRIVE RUN
FDS - FUSIBLE DISCONNECT SWITCH	RFT - REMOTE FAULT TRIP
CB - CIRCUIT BREAKER	LR - INPUT LINE REACTOR
CONTROL:	HAR - PASSIVE HARMONIC FILTER
PN - 3-15 PSI PRESSURE TRANSDUCER	MOL - MULTIPLE MOTOR OVERLOADS

ITEM	INPUT DISC.	DRIVE BYPASS	CONTROL	VOLTAGE			DRIVE		NEMA ENCLOSURE	REMARKS	APPROVED MANUFACTURERS
				INPUT	OUTPUT	PH.	H.P. RATING	TYPE			
VFD-2 EF-1 EF-2 EF-3	DS	3 CONTACT	420 PN	208	208	3	3	PWM	1	SA 'L' VARIABLE TORQUE WITH BYPASS	TOSHIBA C9 SERIES ABB ACH 550 SERIES YASKAWA Z1000 SERIES
VFD-3 EF-4	DS	3 CONTACT	420 PN	208	208	3	3	PWM	1	SA 'L' VARIABLE TORQUE WITH BYPASS	TOSHIBA C9 SERIES ABB ACH 550 SERIES YASKAWA Z1000 SERIES
VFD-15 AHU-10 RETURN	DS	3 CONTACT	420 PN	208	208	3	15	PWM	1	SA 'L' VARIABLE TORQUE WITH BYPASS	TOSHIBA C9 SERIES ABB ACH 550 SERIES YASKAWA Z1000 SERIES
VFD-20 AHU-5.6 RETURN	DS	3 CONTACT	420 PN	208	208	3	20	PWM	1	SA 'L' VARIABLE TORQUE WITH BYPASS	TOSHIBA C9 SERIES ABB ACH 550 SERIES YASKAWA Z1000 SERIES
VFD-25 AHU-10 SUPPLY	DS	3 CONTACT	420 PN	208	208	3	25	PWM	1	SA 'L' VARIABLE TORQUE WITH BYPASS	TOSHIBA C9 SERIES ABB ACH 550 SERIES YASKAWA Z1000 SERIES
VFD-40 AHU-5.6 SUPPLY SCHWP-1,2	DS	3 CONTACT	420 PN	208	208	3	40	PWM	1	SA 'L' VARIABLE TORQUE WITH BYPASS	TOSHIBA C9 SERIES ABB ACH 550 SERIES YASKAWA Z1000 SERIES

**CONFORMED SET
FOR CONSTRUCTION**

PANEL NAME: 5NA										CONNECTED 44 kVA	
TYPE: BOLT-ON					SOLID NEUTRAL GROUND BUS		MAIN: 225 A/MCB				
MOUNTING: Surface							VOLTS: 120/208 Wye				
FED FROM: PANEL DPA					PHASE: 3						
SCCR: 22,000					WIRE: 4						
LOCATION: ELECTRICAL ROOM 5B102					DEMAND: 22.12 kVA						
Panel Notes:											

PANEL NAME: 5C1										CONNECTED 60.8 kVA		
TYPE: BOLT-ON					SOLID NEUTRAL GROUND BUS					MAIN: 225 A/MCB		
MOUNTING: Surface										VOLTS: 120/208 Wye		
FED FROM: PANEL CDP										PHASE: 3		
SCCR: 22,000										WIRE: 4		
LOCATION: ELECTRICAL ROOM 5B102										DEMAND: 25.35 kVA		
Panel Notes:												
CKT NO.	LOAD DESCRIPTION	OVERCURRENT PROTECTION AMPS P	A	B	C	OVERCURRENT PROTECTION AMPS P	LOAD DESCRIPTION	CKT NO.				
5C1-1	OMNICELL	20 A 1	0.24 1.3			1	20 A REFRIGERATOR 5B109	5C1-2				
5C1-3	REC-SB107, 106	20 A 1		0.9 1.2		1	20 A REC-XRAY 5B116	5C1-4				
5C1-5	REC-XRAY 5B117	20 A 1			1.2 1.2	1	20 A REC-XRAY 5B118	5C1-6				
5C1-7	REC-XRAY 5B119	20 A 1	1.2 1.2			1	15 A REC-DENTAL TREAT	5C1-8				
5C1-9	REC-XRAY 5B120	20 A 1		0.18 1.2		1	20 A REC-XRAY 5B121	5C1-10				
5C1-11	REC-XRAY 5B125	20 A 1			1.2 1.2	1	20 A REC-XRAY 5B126	5C1-12				
5C1-13	REC-XRAY 5B127	20 A 1	1.2 1.2			1	15 A REC-DENTAL TREAT	5C1-14				
5C1-15	REC-XRAY 5B123	20 A 1		0.54 0.72		1	20 A REC-5B129	5C1-16				
5C1-17	REC-SB129	20 A 1			0.72 1.2	1	20 A REC-XRAY 5B132	5C1-18				
5C1-19	REC-XRAY 5B133	20 A 1	1.2 1.2			1	20 A REC-XRAY 5B134	5C1-20				
5C1-21	REC-DENTAL TREAT	20 A 1		1.2 1		1	20 A LTS OH LT 5B116	5C1-22				
5C1-23	LTS OH LT 5B117	20 A 1			1 1	1	20 A LTS OH LT 5B118	5C1-24				
5C1-25	LTS OH LT 5B119	20 A 1	1 1			1	20 A LTS OH LT 5B120	5C1-26				
5C1-27	LTS OH LT 5B121	20 A 1		1 1		1	20 A LTS OH LT 5B125	5C1-28				
5C1-29	LTS OH LT 5B126	20 A 1			1 1	1	20 A LTS OH LT 5B127	5C1-30				
5C1-31	LTS OH LT 5B132	20 A 1	1 1			1	20 A LTS OH LT 5B133	5C1-32				
5C1-33	LTS OH LT 5B134	20 A 1		1 0.36		1	20 A REC-CRASH CART 5A115	5C1-34				
5C1-35	REC DOOR 5B100	20 A 1			0.5 0.54	1	20 A REC-SB131, 132, 133	5C1-36				
5C1-37	REC-TELECOMM 5B135	20 A 1	0.9 1.08			1	20 A REC-TELECOMM 5A135	5C1-38				
5C1-39	REC-TELECOMM 5B135	20 A 1		1.08 0.72		1	20 A REC-TELECOMM 5A135	5C1-40				
5C1-41	REC-PAT LIFTS	20 A 1			0.34 0.63	1	20 A LTS DENT LAB	5C1-42				
5C1-43	LTS DENT OP 5B115	20 A 1	1.39 0.98			1	20 A LTS DENT OP 5B115	5C1-44				
5C1-45	LTS DENT OP 5B124	20 A 1		1.18 0.67		1	20 A LTS XRAY WORK	5C1-46				
5C1-47	LTS DENT OP 5B131	20 A 1			1.18 0.02	2	20 A FCU-2 TELECOM 5A135	5C1-48				
5C1-49	PANORAMIC XRAY	20 A 1	1.92 0.02			--	--	5C1-50				
5C1-51	REC-SA111	20 A 1		0.72 1.2		1	15 A DENTAL CHAIR	5C1-52				
5C1-53	DENTAL CHAIR	15 A 1			1.2 1.2	1	15 A DENTAL CHAIR	5C1-54				
5C1-55	DENTAL CHAIR	15 A 1	1.2 1.2			1	15 A DENTAL CHAIR	5C1-56				
5C1-57	DENTAL CHAIR	15 A 1		1.2 1.2		1	20 A REC	5C1-58				
5C1-59	DENTAL CHAIR	15 A 1			1.2 1.2	1	15 A DENTAL CHAIR	5C1-60				
5C1-61	REC-SB131	20 A 1	0 18 1			1	20 A RACK RM 5A135	5C1-62				
5C1-63	DOOR ROOM 5A135	20 A 1		0.5 1		1	20 A RACK RM 5A135	5C1-64				
5C1-65	SPARE	20 A 1			0 0	1	20 A SPARE	5C1-66				
5C1-67	SPARE	20 A 1	0 0			1	20 A SPARE	5C1-68				
5C1-69	SPARE	20 A 1		0 0		1	20 A SPARE	5C1-70				
5C1-71	SPARE	20 A 1			0 0	1	20 A SPARE	5C1-72				
5C1-73	SPARE	20 A 1	0 0			1	20 A SPARE	5C1-74				
5C1-75	SPARE	20 A 1		0 0		1	20 A SPARE	5C1-76				
5C1-77	SPARE	20 A 1			0 0	1	20 A SPARE	5C1-78				
5C1-79	TVSS	60 A 3	0 0			1	20 A SPARE	5C1-80				
5C1-81	--	--		0 0		1	20 A SPARE	5C1-82				
5C1-83	--	--			0 0	1	20 A SPARE	5C1-84				
Total Load:			22.5 kVA	19.63 kVA	18.66 kVA							
Total Amps:			188.76	164.82	155.46							
[Key:]												

A

B

C

D

E

F

5/9/2025 3:03:54 PM

C:\Revit Local Files\ICT_440317_BLDG_1_Electrical\ODS_Jason.C.Meyer.rvt

TYPE: BOLT-ON

MOUNTING: Surface

FED FROM: PANEL DPB

SCCR: 22,000

LOCATION: ELECTRICAL ROOM 3B101

PANEL NAME: 3NB

CONNECTED 24.6 KVA

MAIN: 225 A/MCB

VOLTS: 120/208 Wye

PHASE: 3

WIRE: 4

DEMAND: 11.44 KVA

SOLID NEUTRAL

GROUND BUS

Panel Notes:

CKT NO.	LOAD DESCRIPTION	OVERCURRENT PROTECTION AMPS	A	B	C	OVERCURRENT PROTECTION AMPS	LOAD DESCRIPTION	CKT NO.
3NB-1	REC-BATH 3B114	20 A	1	1.93	0.5		20 A HEADWALL 3B114	3NB-2
3NB-3	HEADWALL 3B117	20 A	1		0.5	0.88	1 20 A REC-BATH 3B117	3NB-4
3NB-5	HEADWALL 3B116	20 A	1			0.5	1 20 A REC-3B101 CORR	3NB-6
3NB-7	REC-3B103	20 A	1	1.26	1.08		1 20 A REC-3B103	3NB-8
3NB-9	REC-3B103	20 A	1		1.08	1.08	1 20 A REC-3B103	3NB-10
3NB-11	REC	20 A	1			0.9	1 20 A REC-3B103	3NB-12
3NB-13	REC	20 A	1	1.08	1.26		1 20 A REC-3B113	3NB-14
3NB-15	REC-3B113	20 A	1		1.08	0.5	1 20 A HEADWALL 3B124	3NB-16
3NB-17	REC-3B124 BATH	20 A	1			0.88	1 20 A HEADWALL 3B123	3NB-18
3NB-19	REC-3B123 BATH	20 A	1	0.88	0.88		1 20 A REC-3B119	3NB-20
3NB-21	HEADWALL 3B119	20 A	1		0.5	1.23	1 20 A REC-3B111	3NB-22
3NB-23	REC-3B111A BATH	20 A	1			0.18	1 20 A HEADWALL 3B111	3NB-24
3NB-25	REC	20 A	1	0.54	0.69		1 20 A LTS-WHEELCHAIR, CORR	3NB-26
3NB-27	LTS-NURSE 3B125	20 A	1		0.4	0.29	1 20 A LTS-3B118, 119, 121	3NB-28
3NB-29	LTS-3B123, 3B124	20 A	1			0.2	1 20 A SPARE	3NB-30
3NB-31	SPARE	20 A	1	0	0.21		1 20 A LTS-3B114, 116	3NB-32
3NB-33	LTS-3B123, 3B124	20 A	1		0.42	0.3	1 20 A VAV BOXES	3NB-34
3NB-35	SPARE	20 A	1			0	1 20 A SPARE	3NB-36
3NB-37	SPARE	20 A	1	0	0		1 20 A SPARE	3NB-38
3NB-39	SPARE	20 A	1		0	0	1 20 A SPARE	3NB-40
3NB-41	SPARE	20 A	1			0	1 20 A SPARE	3NB-42
3NB-43	SPARE	20 A	1	0	0		1 20 A SPARE	3NB-44
3NB-45	SPARE	20 A	1		0	0	1 20 A SPARE	3NB-46
3NB-47	SPARE	20 A	1			0	1 20 A SPARE	3NB-48
3NB-49	SPARE	20 A	1	0	0		1 20 A SPARE	3NB-50
3NB-51	SPARE	20 A	1		0	0	1 20 A SPARE	3NB-52
3NB-53	SPARE	20 A	1			0	1 20 A SPARE	3NB-54
3NB-55	SPARE	20 A	1	0	0		1 20 A SPARE	3NB-56
3NB-57	SPARE	20 A	1		0	0	1 20 A SPARE	3NB-58
3NB-59	SPARE	20 A	1			0	1 20 A SPARE	3NB-60
Total Load:			10.25 KVA			8.2 KVA		
Total Amps:			88.03			70.97		
						6.15 KVA		
						51.28		
[Key*:]								

TYPE: BOLT-ON

MOUNTING: SURFACE

FED FROM: EXISTING 500KW GENERATOR

LOCATION: ELECTRICAL ROOM 6B100A

SCCR: 22,000

DISCONNECT TYPE: FS - HEAVY DUTY FUSED SWITCH
BPS - BOLTED PRESSURE SWITCH
MCB - MOLDED CASE BREAKER
ECB - ELECTRONIC TRIP BREAKER
CLB - CURRENT LIMITING BREAKER
ICB - INSULATED CASE BREAKER

DISTRIBUTION PANEL: EDP

MAIN: 1200 A /MCB

VOLTS: 120/208 Wye

PHASE: 3

WIRE: 4

DEMAND: 292894 VA

SOLID NEUTRAL

GROUND BUS

ACCESSORIES:
DPM - DIGITAL POWER METER
GFI - GROUND FAULT PROTECTION
ST - SHUNT TRIP (120V COIL)
Z1 - ZONE INTERLOCK

Notes: PROVIDE ZONE INTERLOCK ARC REDUCTION ON MAIN CIRCUIT BREAKER

CKT	LOAD DESCRIPTION	Load	FRAME	POLES	TRIP RATING	TYPE	ACCESSORIES
EDP-1	L.S. ATS	13.17 kVA	400 A	3	100 A		
EDP-2							
EDP-3	EQ. ATS	304.58 kVA	900 A	3	900 A		
EDP-4							
EDP-5							
EDP-6		0 kVA	400 A	3	100 A		
EDP-7	TVSS	317.15 kVA	TOTAL KVA				

TYPE: BOLT-ON

MOUNTING: SURFACE

FED FROM: L.S. ATS

LOCATION: ELECTRICAL ROOM 6B100A

SCCR: 25,000

DISCONNECT TYPE: FS - HEAVY DUTY FUSED SWITCH
BPS - BOLTED PRESSURE SWITCH
MCB - MOLDED CASE BREAKER
ECB - ELECTRONIC TRIP BREAKER
CLB - CURRENT LIMITING BREAKER
ICB - INSULATED CASE BREAKER

DISTRIBUTION PANEL: LSDP

MAIN: 100 A M.C.B.

VOLTS: 120/208 Wye

PHASE: 3

WIRE: 4

DEMAND: 8783 VA

SOLID NEUTRAL

GROUND BUS

ACCESSORIES:
DPM - DIGITAL POWER METER
GFI - GROUND FAULT PROTECTION
ST - SHUNT TRIP (120V COIL)
Z1 - ZONE INTERLOCK

Notes:

CKT	LOAD DESCRIPTION	Load	FRAME	POLES	TRIP RATING	TYPE	ACCESSORIES
LSDP-1	5LS1	5.56 kVA	100 A	3	60 A		
LSDP-2	3LS1	7.62 kVA	100 A	3	60 A		
LSDP-3							
LSDP-4							
LSDP-5			100 A	3			
LSDP-6		12.67 kVA	TOTAL KVA				

TYPE: BOLT-ON

MOUNTING: SURFACE

FED FROM: CRITICAL ATS

LOCATION: 22,000

DISCONNECT TYPE: FS - HEAVY DUTY FUSED SWITCH
BPS - BOLTED PRESSURE SWITCH
MCB - MOLDED CASE BREAKER
ECB - ELECTRONIC TRIP BREAKER
CLB - CURRENT LIMITING BREAKER
ICB - INSULATED CASE BREAKER

DISTRIBUTION PANEL: CDP

MAIN: 600 A /MCB

VOLTS: 120/208 Wye

PHASE: 3

WIRE: 4

DEMAND: 39744 VA

SOLID NEUTRAL

GROUND BUS

ACCESSORIES:
DPM - DIGITAL POWER METER
GFI - GROUND FAULT PROTECTION
ST - SHUNT TRIP (120V COIL)
Z1 - ZONE INTERLOCK

Notes:

CKT	LOAD DESCRIPTION	Load	FRAME	POLES	TRIP RATING	TYPE	ACCESSORIES
CDP-1	PANEL 3C1	43.37 kVA	400 A	3	125 A		
CDP-2	PANEL 4C1	39.56 kVA	400 A	3	125 A		
CDP-3							
CDP-4							
CDP-5							
CDP-6							
CDP-7	TVSS	0 kVA	400 A	3	100 A		
		82.94 kVA	TOTAL KVA				

TYPE: BOLT-ON

MOUNTING: SURFACE

FED FROM: EXISTING GE TIE A

LOCATION: ELECTRICAL ROOM 6B100B

SCCR: 25,000

DISCONNECT TYPE: FS - HEAVY DUTY FUSED SWITCH
BPS - BOLTED PRESSURE SWITCH
MCB - MOLDED CASE BREAKER
ECB - ELECTRONIC TRIP BREAKER
CLB - CURRENT LIMITING BREAKER
ICB - INSULATED CASE BREAKER

DISTRIBUTION PANEL: DPA

MAIN: 1200 A /MCB

VOLTS: 120/208 Wye

PHASE: 3

WIRE: 4

DEMAND: 79824 VA

SOLID NEUTRAL

GROUND BUS

ACCESSORIES:
DPM - DIGITAL POWER METER
GFI - GROUND FAULT PROTECTION
ST - SHUNT TRIP (120V COIL)
Z1 - ZONE INTERLOCK

Notes: PROVIDE ZONE INTERLOCK ARC REDUCTION ON MAIN CIRCUIT BREAKER

CKT	LOAD DESCRIPTION	Load	FRAME	POLES	TRIP RATING	TYPE	ACCESSORIES
DPA-1	3NA	30.9 kVA	400 A	3	225 A		
DPA-2							
DPA-3	5NA	44.01 kVA	400 A	3	225 A		
DPA-4	CRITICAL ATS	82.94 kVA	800 A	3	600 A		
DPA-5							
DPA-6							
DPA-7							
DPA-8							
DPA-9							
DPA-10	VAV BOXES IN ATTIC	0.1 kVA	60 A	1	20 A		
DPA-11	FCU 4,5	1.07 kVA	60 A	2	20 A		
DPA-12			100 A	3			
		159.02 kVA	TOTAL KVA				

TYPE: BOLT-ON

MOUNTING: SURFACE

FED FROM: EXISTING GE TIE B

LOCATION: ELECTRICAL ROOM 6B100B

SCCR: 25,000

DISCONNECT TYPE: FS - HEAVY DUTY FUSED SWITCH
BPS - BOLTED PRESSURE SWITCH
MCB - MOLDED CASE BREAKER
ECB - ELECTRONIC TRIP BREAKER
CLB - CURRENT LIMITING BREAKER
ICB - INSULATED CASE BREAKER

DISTRIBUTION PANEL: DPB

MAIN: 1200 A /MCB

VOLTS: 120/208 Wye

PHASE: 3

WIRE: 4

DEMAND: 48786 VA

SOLID NEUTRAL

GROUND BUS

ACCESSORIES:
DPM - DIGITAL POWER METER
GFI - GROUND FAULT PROTECTION
ST - SHUNT TRIP (120V COIL)
Z1 - ZONE INTERLOCK

Notes: PROVIDE ZONE INTERLOCK ARC REDUCTION ON MAIN CIRCUIT BREAKER

CKT	LOAD DESCRIPTION	Load	FRAME	POLES	TRIP RATING	TYPE	ACCESSORIES
DPB-1	PANEL 3NB	24.6 kVA	400 A	3	225 A		
DPB-2	PANEL 4NB	25.09 kVA	400 A	3	225 A		
DPB-3	PANEL 5NB	44.28 kVA	400 A	3	225 A		
DPB-4							
DPB-5	BCU-1	1.66 kVA	60 A	3	15 A		
DPB-6							
DPB-7							
DPB-8							
DPB-9							
DPB-10							
DPB-11							
DPB-12							
DPB-13							
DPB-14	TVSS	0 kVA	400 A	3	100 A		
		95.01 kVA	TOTAL KVA				

Revisions:	Date:

CONSULTANT



623 26th Avenue
Rock Island, IL 61201
T: 309.788.0673
F: 309.786.5967

ARCHITECT/ENGINEER OF RECORD



13605 1st Ave. N. #100 Plymouth, MN 55441
P 763.412.4000 | F 763.412.4090 | ae-mn.com
Anderson Engineering of Minnesota, LLC | Proj #

STAMP



Office of Construction and Facilities Management

 U.S. Department of Veterans Affairs

Drawing Title

PANEL SCHEDULES - ELECTRICAL

Approved:

Phase

CONSTRUCTION DOCUMENTS

FULLY SPRINKLERED

Project Title

RENOVATE BUILDING 1

Location

BILOXI, MISSISSIPPI

Issue Date

05/12/2025

Checked

IMEG

Drawn

STEWIE

Project Number

520-317X

Building Number

1

Drawing Number

E404

Dwg. 230 of 239

CONFORMED SET
FOR CONSTRUCTION

05-12-2025
Exp. 12-31-2025

PANEL NAME: 4NA										CONNECTED 32.6 kVA		
TYPE: BOLT-ON				SOLID NEUTRAL				MAIN: 225 A/MCB				
MOUNTING: Surface								VOLTS: 120/208 Wye				
FED FROM: PANEL DPA								PHASE: 3				
SCCR: 22,000								WIRE: 4				
LOCATION: ELECTRICAL ROOM 4B101								DEMAND: 19.41 kVA				
Panel Notes:												
CKT NO.	LOAD DESCRIPTION	OVERCURRENT PROTECTION AMPS	P	A	B	C	OVERCURRENT PROTECTION AMPS	P	LOAD DESCRIPTION	CKT NO.		
4NA-1	REC-4A106	20 A	1	0.72	0.72		1	20 A	REC-4A101, 105	4NA-2		
4NA-3	REC-4A102, 103, 104	20 A	1		0.54	0.18	1	20 A	REC-VENDING	4NA-4		
4NA-5	REC-VENDING	20 A	1			0.18	0.9	1	20 A	REC-4A109, 110, 111	4NA-6	
4NA-7	REC-4A112, 114, 115	20 A	1	0.9	1.2		1	20 A	REC-COPIER 4A112	4NA-8		
4NA-9	REC-COPIER	20 A	1		1.2	0	1	20 A	SPARE	4NA-10		
4NA-11	REC-4A114, 115	20 A	1			0.72	0.18	1	20 A	ICE MAKER	4NA-12	
4NA-13	MICROWAVE	20 A	1	0.8	1.08			1	20 A	REC-4A116, 140	4NA-14	
4NA-15	REC-4A137	20 A	1		0.36	1.3		1	20 A	REFRIG-4A137	4NA-16	
4NA-17	MICRO-4A137	20 A	1			0.8	0.9	1	20 A	REC-4A136, 137, 138&41	4NA-18	
4NA-19	REC-4A137, 133	20 A	1	1.08	0.72		1	20 A	REC-4A133	4NA-20		
4NA-21	REC-4A134, 135	20 A	1		0.36	0.18	1	20 A	REC-BATH 4A142	4NA-22		
4NA-23	HEADWALL-4A130	20 A	1			0.5	1.41	1	20 A	REC-BATH 4A130	4NA-24	
4NA-25	REC-4A129	20 A	1	1.26	1.08			1	20 A	REC-4A128	4NA-26	
4NA-27	REC-4A125, 128	20 A	1		1.23	0.5		1	20 A	HEADWALL-4A125	4NA-28	
4NA-29	REC-4A123	20 A	1			0.88	0.5	1	20 A	HEADWALL-4A123	4NA-30	
4NA-31	HEADWALL-4A122	20 A	1	0.5	0.88			1	20 A	REC-4A122	4NA-32	
4NA-33	REC-4A121	20 A	1		0.54	0.5		1	20 A	HEADWALL-4A118	4NA-34	
4NA-35	REC	20 A	1			0.88	0.88	1	20 A	REC-4A117	4NA-36	
4NA-37	HEADWALL-4A117	20 A	1	0.5	0.32			1	20 A	LTS-4A138, 139, 141	4NA-38	
4NA-39	REC-4B121	20 A	1		1.08	0.43		1	20 A	LTS-4A130, 131, 134	4NA-40	
4NA-41	LTS-4A128, 127, 124&5	20 A	1			0.34	0.2	1	20 A	LTS-4A122, 123	4NA-42	
4NA-43	LTS-4A117, 118	20 A	1	0.29	0.69			1	20 A	LTS-CORRIDOR C4-103,104,4A105,4A106	4NA-44	
4NA-45	LTS-SCONCES 4A100	20 A	1		0.6	0.15		1	20 A	LTS-CORRIDOR C4-106	4NA-46	
4NA-47	LTS-COORIDOR C4-107,108,109	20 A	1			0.15	0	1	20 A	SPARE	4NA-48	
4NA-49	LTS-SCONCES 4A116	20 A	1	0.5	0.06			1	20 A	LTS-4A106	4NA-50	
4NA-51	VAV BOXES CORR, LOBBY	20 A	1		0.4	0.35		1	20 A	VAV BOXES LKRS, LNG	4NA-52	
4NA-53	SPARE	20 A	1				0	0.18	1	20 A	MONITOR-4A128	4NA-54
4NA-55	VAV BOXES 4A121	20 A	1	0.05	0			1	20 A	SPARE	4NA-56	
4NA-57	SPARE	20 A	1		0	0		1	20 A	SPARE	4NA-58	
4NA-59	SPARE	20 A	1			0	0	1	20 A	SPARE	4NA-60	
4NA-61	SPARE	20 A	1	0	0			1	20 A	SPARE	4NA-62	
4NA-63	SPARE	20 A	1		0	0		1	20 A	SPARE	4NA-64	
4NA-65	SPARE	20 A	1			0	0	1	20 A	SPARE	4NA-66	
4NA-67	SPARE	20 A	1	0	0			1	20 A	SPARE	4NA-68	
4NA-69	SPARE	20 A	1		0	0		1	20 A	SPARE	4NA-70	
4NA-71	SPARE	20 A	1			0	0	1	20 A	SPARE	4NA-72	
4NA-73	SPARE	20 A	1	0	0			1	20 A	SPARE	4NA-74	
4NA-75	SPARE	20 A	1		0	0		1	20 A	SPARE	4NA-76	
4NA-77	SPARE	20 A	1			0	0	1	20 A	SPARE	4NA-78	
4NA-79	SPARE	20 A	1	0	0			1	20 A	SPARE	4NA-80	
4NA-81	SPARE	20 A	1		0	0		1	20 A	SPARE	4NA-82	
4NA-83	SPARE	20 A	1			0	0	1	20 A	SPARE	4NA-84	
Total Load:				13.26 kVA	9.85 kVA	9.54 kVA						
Total Amps:				110.87	82.44	79.54						
[Key:-] *G = GFCI BREAKER												

PANEL NAME: 4NB										CONNECTED 25.1 KVA	
TYPE: BOLT-ON				SOLID NEUTRAL				MAIN: 225 A/MCB			
MOUNTING: Surface								VOLTS: 120/208 Wye			
FED FROM: PANEL DPB								PHASE: 3			
SCCR: 22,000								WIRE: 4			
LOCATION: ELECTRICAL ROOM 4B101								DEMAND: 11.6 KVA			
Panel Notes:											
CKT NO.	LOAD DESCRIPTION	OVERCURRENT T PROTECTION AMPS	P	A	B	C	OVERCURRENT T PROTECTION P	AMPS	LOAD DESCRIPTION	CKT NO.	
4NB-1	WATER COOLER	20 A	1	0.5	0.5		1	20 A	HEADWALL-4B111	4NB-2	
4NB-3	HEADWALL-4B124	20 A	1		0.5	0.88	1	20 A	REC-4B124	4NB-4	
4NB-5	REC-4B123	20 A	1			0.88	0.5	1	20 A	HEADWALL-4B123	4NB-6
4NB-7	REC-4B119	20 A	1	0.88	0.5		1	20 A	HEADWALL-4B119	4NB-8	
4NB-9	HEADWALL-4B118	20 A	1		0.5	0.88	1	20 A	REC-4B118	4NB-10	
4NB-11	HEADWALL-4B116	20 A	1			0.5	1.93	1	20 A	REC-4B114, 116	4NB-12
4NB-13	HEADWALL-4B114	20 A	1	0.5	1.26		1	20 A	REC-4B113	4NB-14	
4NB-15	REC-4B113	20 A	1		1.08	1.41	1	20 A	REC-4B111	4NB-16	
4NB-17	REC-4B106, 110	20 A	1			0.9	1.08	1	20 A	REC-4B102, 106, 107	4NB-18
4NB-19	REC-4B109	20 A	1	0.9	1.08		1	20 A	REC-4B109	4NB-20	
4NB-21	REC-4B109	20 A	1		1.08	1.08	1	20 A	REC-4B103	4NB-22	
4NB-23	REC-4B103	20 A	1			1.08	1.08	1	20 A	REC-4B103	4NB-24
4NB-25	REC-4B103	20 A	1	0.72	0.52		1	20 A	LTS-CORRIDOR C4-100,101,102	4NB-26	
4NB-27	SPARE	20 A	1		0	0	1	20 A	SPARE	4NB-28	
4NB-29	LTS-4B111, 113	20 A	1			0.42	0.21	1	20 A	LTS-4B114, 116	4NB-30
4NB-31	LTS-4B118, 119	20 A	1	0.29	0.2		1	20 A	LTS-4B123, 124	4NB-32	
4NB-33	LTS-4B100 CORR SCOR	20 A	1		0.6	0.25		1	20 A	VAV BOXES	4NB-34
4NB-35	REC-4A105	20 A	1			0.54	0	1	20 A	SPARE	4NB-36
4NB-37	SPARE	20 A	1	0	0		1	20 A	SPARE	4NB-38	
4NB-39	SPARE	20 A	1		0	0	1	20 A	SPARE	4NB-40	
4NB-41	SPARE	20 A	1			0	0	1	20 A	SPARE	4NB-42
4NB-43	SPARE	20 A	1	0	0		1	20 A	SPARE	4NB-44	
4NB-45	SPARE	20 A	1		0	0	1	20 A	SPARE	4NB-46	
4NB-47	SPARE	20 A	1			0	0	1	20 A	SPARE	4NB-48
4NB-49	SPARE	20 A	1	0	0		1	20 A	SPARE	4NB-50	
4NB-51	SPARE	20 A	1		0	0	1	20 A	SPARE	4NB-52	
4NB-53	SPARE	20 A	1			0	0	1	20 A	SPARE	4NB-54
4NB-55	SPARE	20 A	1	0	0		1	20 A	SPARE	4NB-56	
4NB-57	SPARE	20 A	1		0	0	1	20 A	SPARE	4NB-58	
4NB-59	SPARE	20 A	1			0	0	1	20 A	SPARE	4NB-60
Total Load:				7.8 kVA	8.22 kVA	9.07 kVA					
Total Amps:				64.96	69.03	76.16					
[Key:-] *G = GFCI BREAKER											

DISTRIBUTION PANEL:				EQDP							
TYPE: BOLT-ON		SURFACE		SOLID NEUTRAL				MAIN: 900 A /MCB			
MOUNTING: SURFACE				GROUND BUS				VOLTS: 120/208 Wye			
FED FROM: EQUIP. ATS								PHASE: 3			
LOCATION:								WIRE: 4			
SCCR: 22,000								DEMAND: 284137 VA			
DISCONNECT TYPE:				ACCESSORIES:							
FS - HEAVY DUTY FUSED SWITCH				DPM - DIGITAL POWER METER							
BPS - BOLTED PRESSURE SWITCH				GFI - GROUND FAULT PROTECTION							
MCB - MOLDED CASE BREAKER				ST - SHUNT TRIP (120V COIL)							
ECB - ELECTRONIC TRIP BREAKER				ZI - ZONE INTERLOCK							
CLB - CURRENT LIMITING BREAKER											
ICB - INSULATED CASE BREAKER											
Notes:											
CKT	LOAD DESCRIPTION	Load	FRAME	POLES	TRIP RATING	TYPE	ACCESSORIES				
EQDP-1	AHU-5 RETURN	18.14 kVA	100 A	3	100 A						
EQDP-2	AHU-6 RETURN	18.14 kVA	100 A	3	100 A						
EQDP-3	EF-1 (TB) WEST	2.49 kVA	60 A	3	15 A						
EQDP-4	AHU-5 SUPPLY	35.15 kVA	400 A	3	175 A						
EQDP-5	AHU-10 SUPPLY	23.2 kVA	400 A	3	110 A						
EQDP-6	AHU-6 SUPPLY	35.15 kVA	400 A	3	175 A						
EQDP-7	EXISTING EF-7 1/4HP ELEV VENT...	0.31 kVA	60 A	3	20 A						
EQDP-8	EF-2 (TB) EAST	2.49 kVA	60 A	3	15 A						
EQDP-9	CONNECTOR DAC-1	23.2 kVA	60 A	3	20 A						
EQDP-10	PAL HEAT	2.25 kVA	100 A	3	100 A						
EQDP-11	MVP-1 MED VAC PMPs	12.81 kVA	60 A	3	60 A						
EQDP-12	CONNECTOR MAC-1	18.23 kVA	60 A	3	20 A						
EQDP-13	AHU-10 RETURN	14.58 kVA	100 A	3	90 A						
EQDP-14	30 HP ELEV	33.15 kVA	400 A	3	200 A						
EQDP-15	AIR-DRYER	1.56 kVA	60 A	3	20 A						
EQDP-16	40 HP ELEV	43.23 kVA	400 A	3	250 A						
EQDP-17	EF-3 EXISTING	3.96 kVA	60 A	3	20 A						
EQDP-18	ELEVATOR LTS.PWR	1 KVA	60 A	1	20 A						
EQDP-19											
EQDP-20	EXIST 1.5 TON A/C	4.99 kVA	60 A	3	30 A						
EQDP-21											
EQDP-22											
EQDP-23	EF-1 EXISTING	3.96 kVA	60 A	3	20 A						
EQDP-24											
EQDP-25	EF-3 GEN WEST	2.81 kVA	60 A	3	15 A						
EQDP-26	EF-4 GEN EAST	3.96 kVA	60 A	3	20 A						
EQDP-27											
EQDP-28	TVSS	0 KVA	100 A	3	100 A						
		304.58 kVA	TOTAL KVA								