


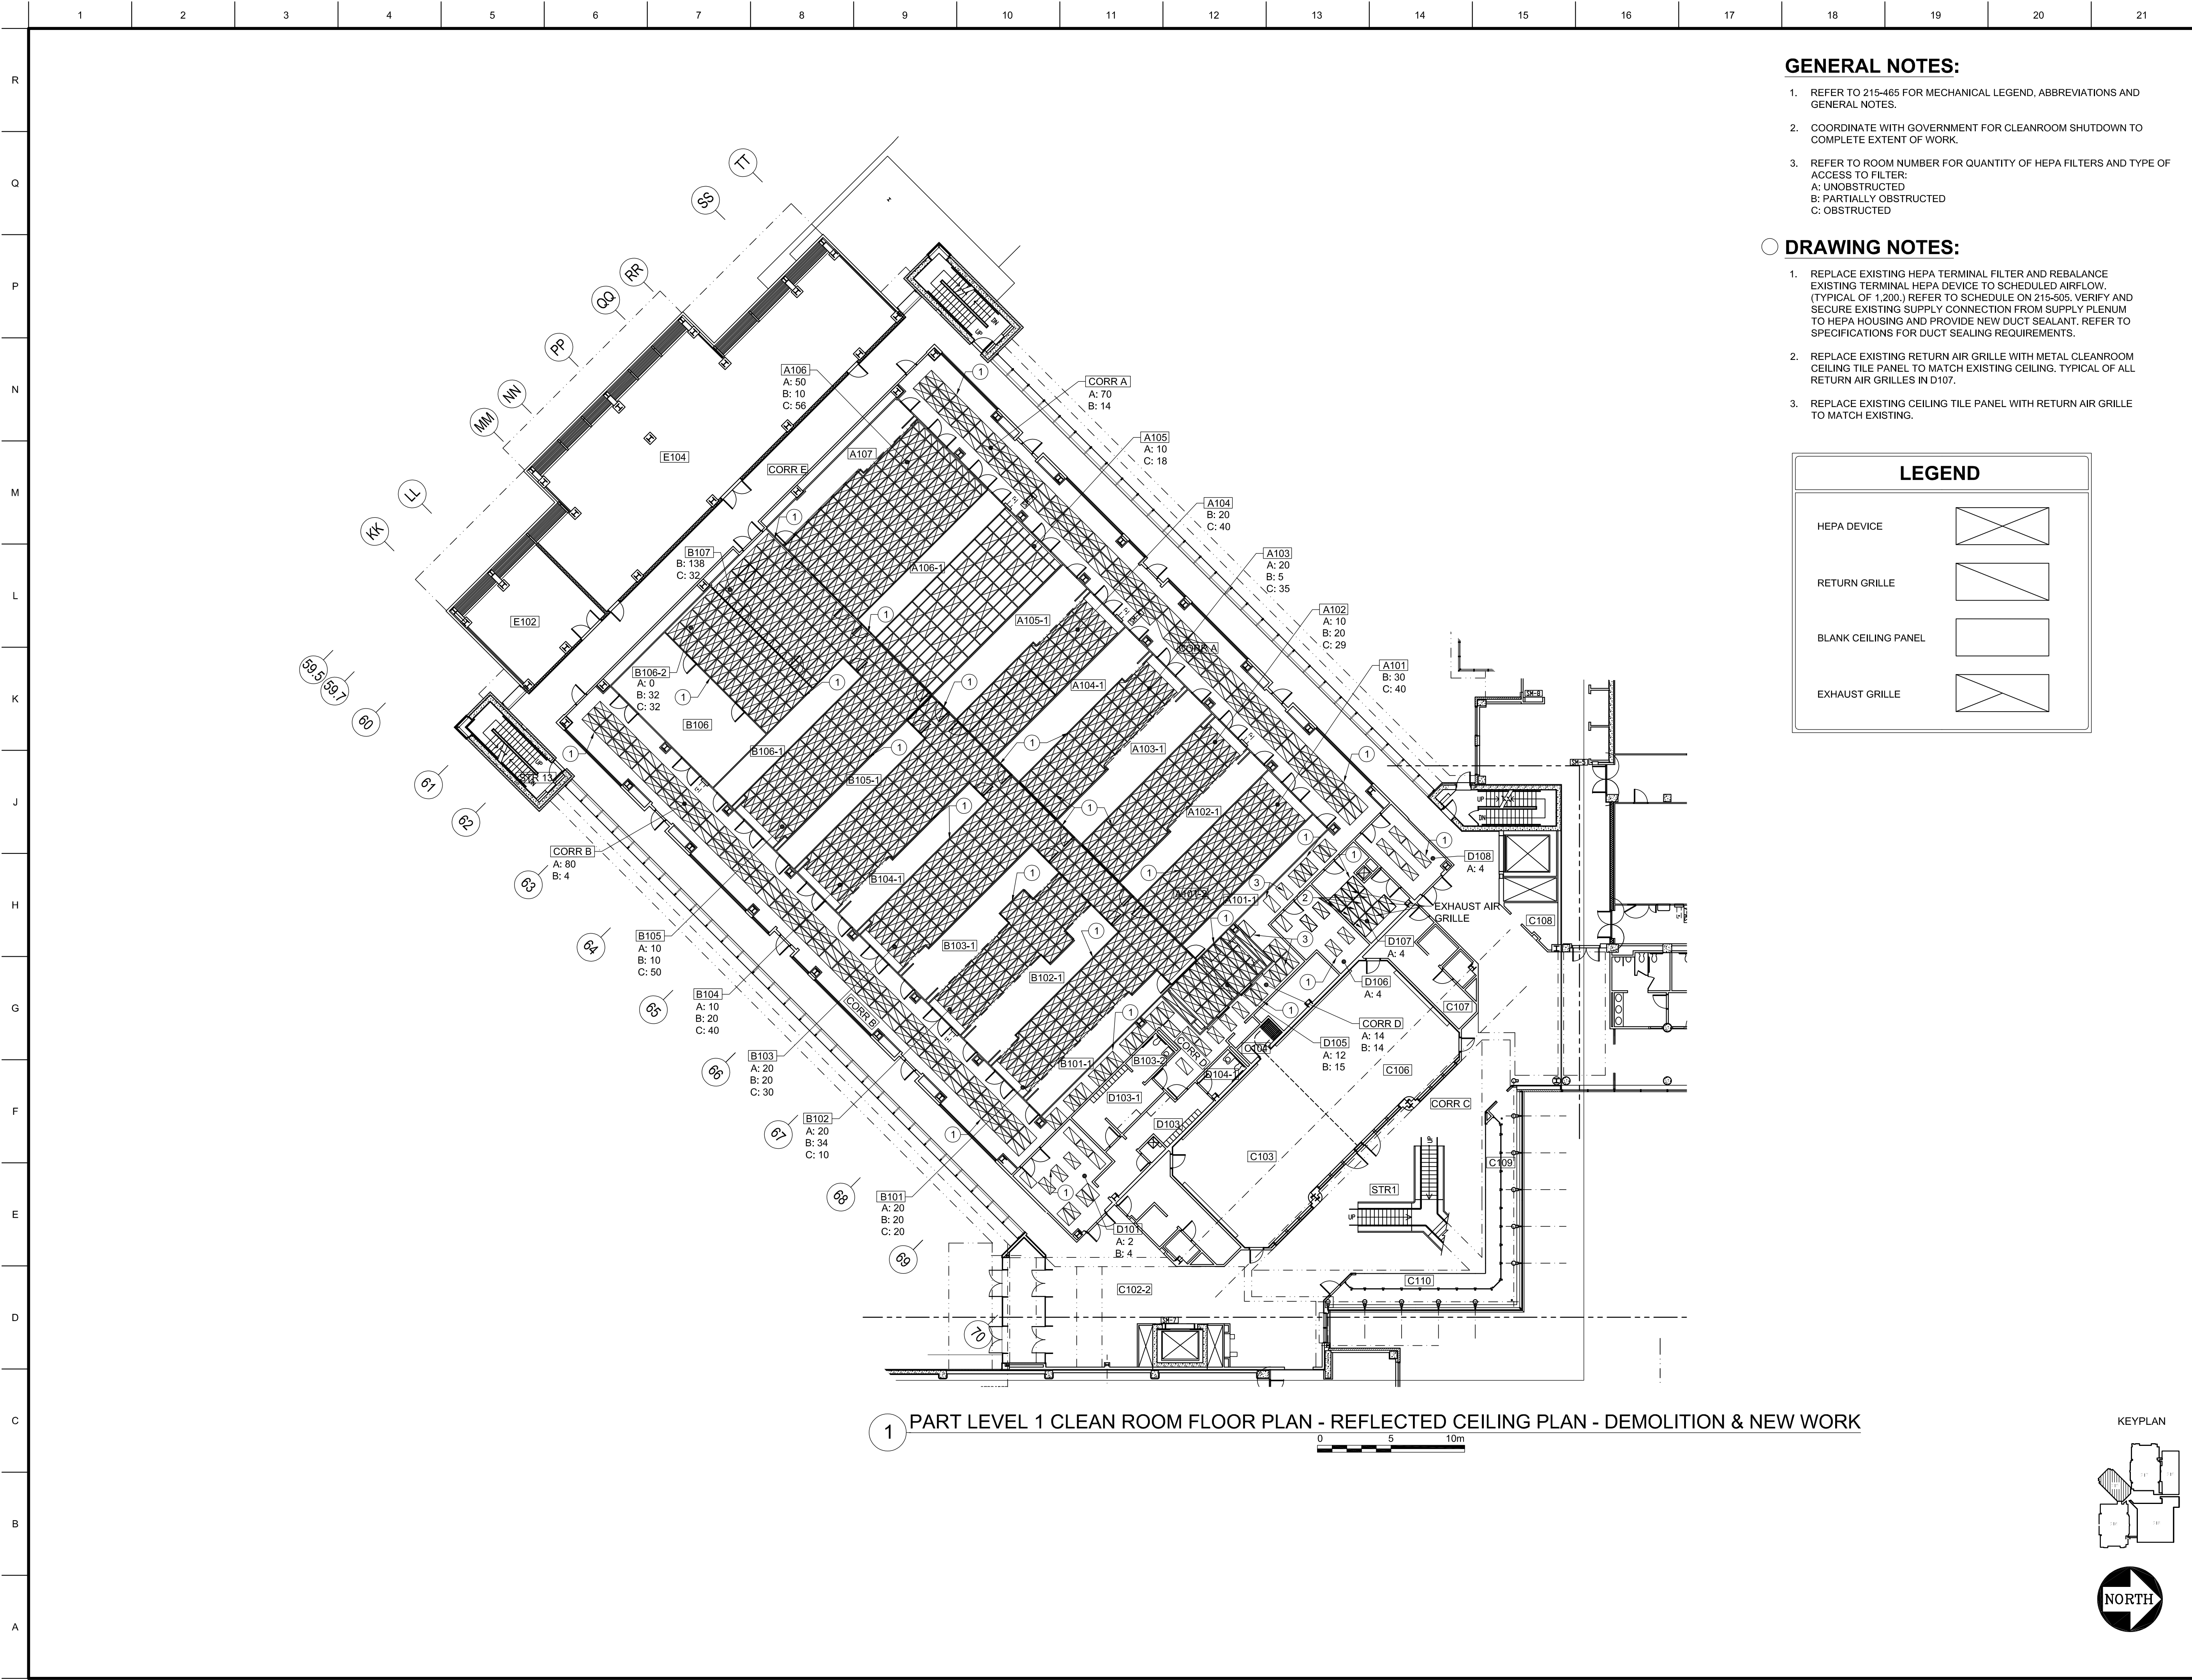

GENERAL NOTES:

- REFER TO 215-465 FOR MECHANICAL LEGEND, ABBREVIATIONS AND GENERAL NOTES.
- COORDINATE WITH GOVERNMENT FOR CLEANROOM SHUTDOWN TO COMPLETE EXTENT OF WORK.
- REFER TO ROOM NUMBER FOR QUANTITY OF HEPA FILTERS AND TYPE OF ACCESS TO FILTER:
A: UNOBSTRUCTED
B: PARTIALLY OBSTRUCTED
C: OBSTRUCTED

DRAWING NOTES:

- REPLACE EXISTING HEPA TERMINAL FILTER AND REBALANCE EXISTING TERMINAL HEPA DEVICE TO SCHEDULED AIRFLOW. (TYPICAL OF 1,200.) REFER TO SCHEDULE ON 215-305. VERIFY AND SECURE EXISTING SUPPLY CONNECTION FROM SUPPLY PLENUM TO HEPA HOUSING AND PROVIDE NEW DUCT SEALANT. REFER TO SPECIFICATIONS FOR DUCT SEALING REQUIREMENTS.
- REPLACE EXISTING RETURN AIR GRILLE WITH METAL CLEANROOM CEILING TILE PANEL TO MATCH EXISTING CEILING. TYPICAL OF ALL RETURN AIR GRILLES IN D107.
- REPLACE EXISTING CEILING TILE PANEL WITH RETURN AIR GRILLE TO MATCH EXISTING.

LEGEND

- | | |
|---------------------|--|
| HEPA DEVICE | |
| RETURN GRILLE | |
| BLANK CEILING PANEL | |
| EXHAUST GRILLE | |

100% RELEASE FOR CONSTRUCTION

ISSUE DATE: JUNE 28, 2021	DESIGNED BY: J. METZLER	NIST OFPM	GAITHERSBURG, MD
SOLICITATION NO.: 68147-000003	DRAWN BY: A. GADEMAN	BURDETTE, KOEHLER, MURPHY & ASSOCIATES, INC.	6300 BLAIR HILL LANE, SUITE 400 BALTIMORE, MARYLAND 21209
CYCLE NO.: NO 000001-04225	CHECKED BY: C. G. G. G.		
	SUBMITTED BY: BNA		
	SIZE: A1		

GAITHERSBURG, MD BUILDING 215
CLEANROOM REBALANCE
CLIN 0003
19W08375

PART LEVEL 1 CLEAN ROOM FLOOR PLAN
CEILING
DEMOLITION & NEW WORK

SHEET ID
215-468