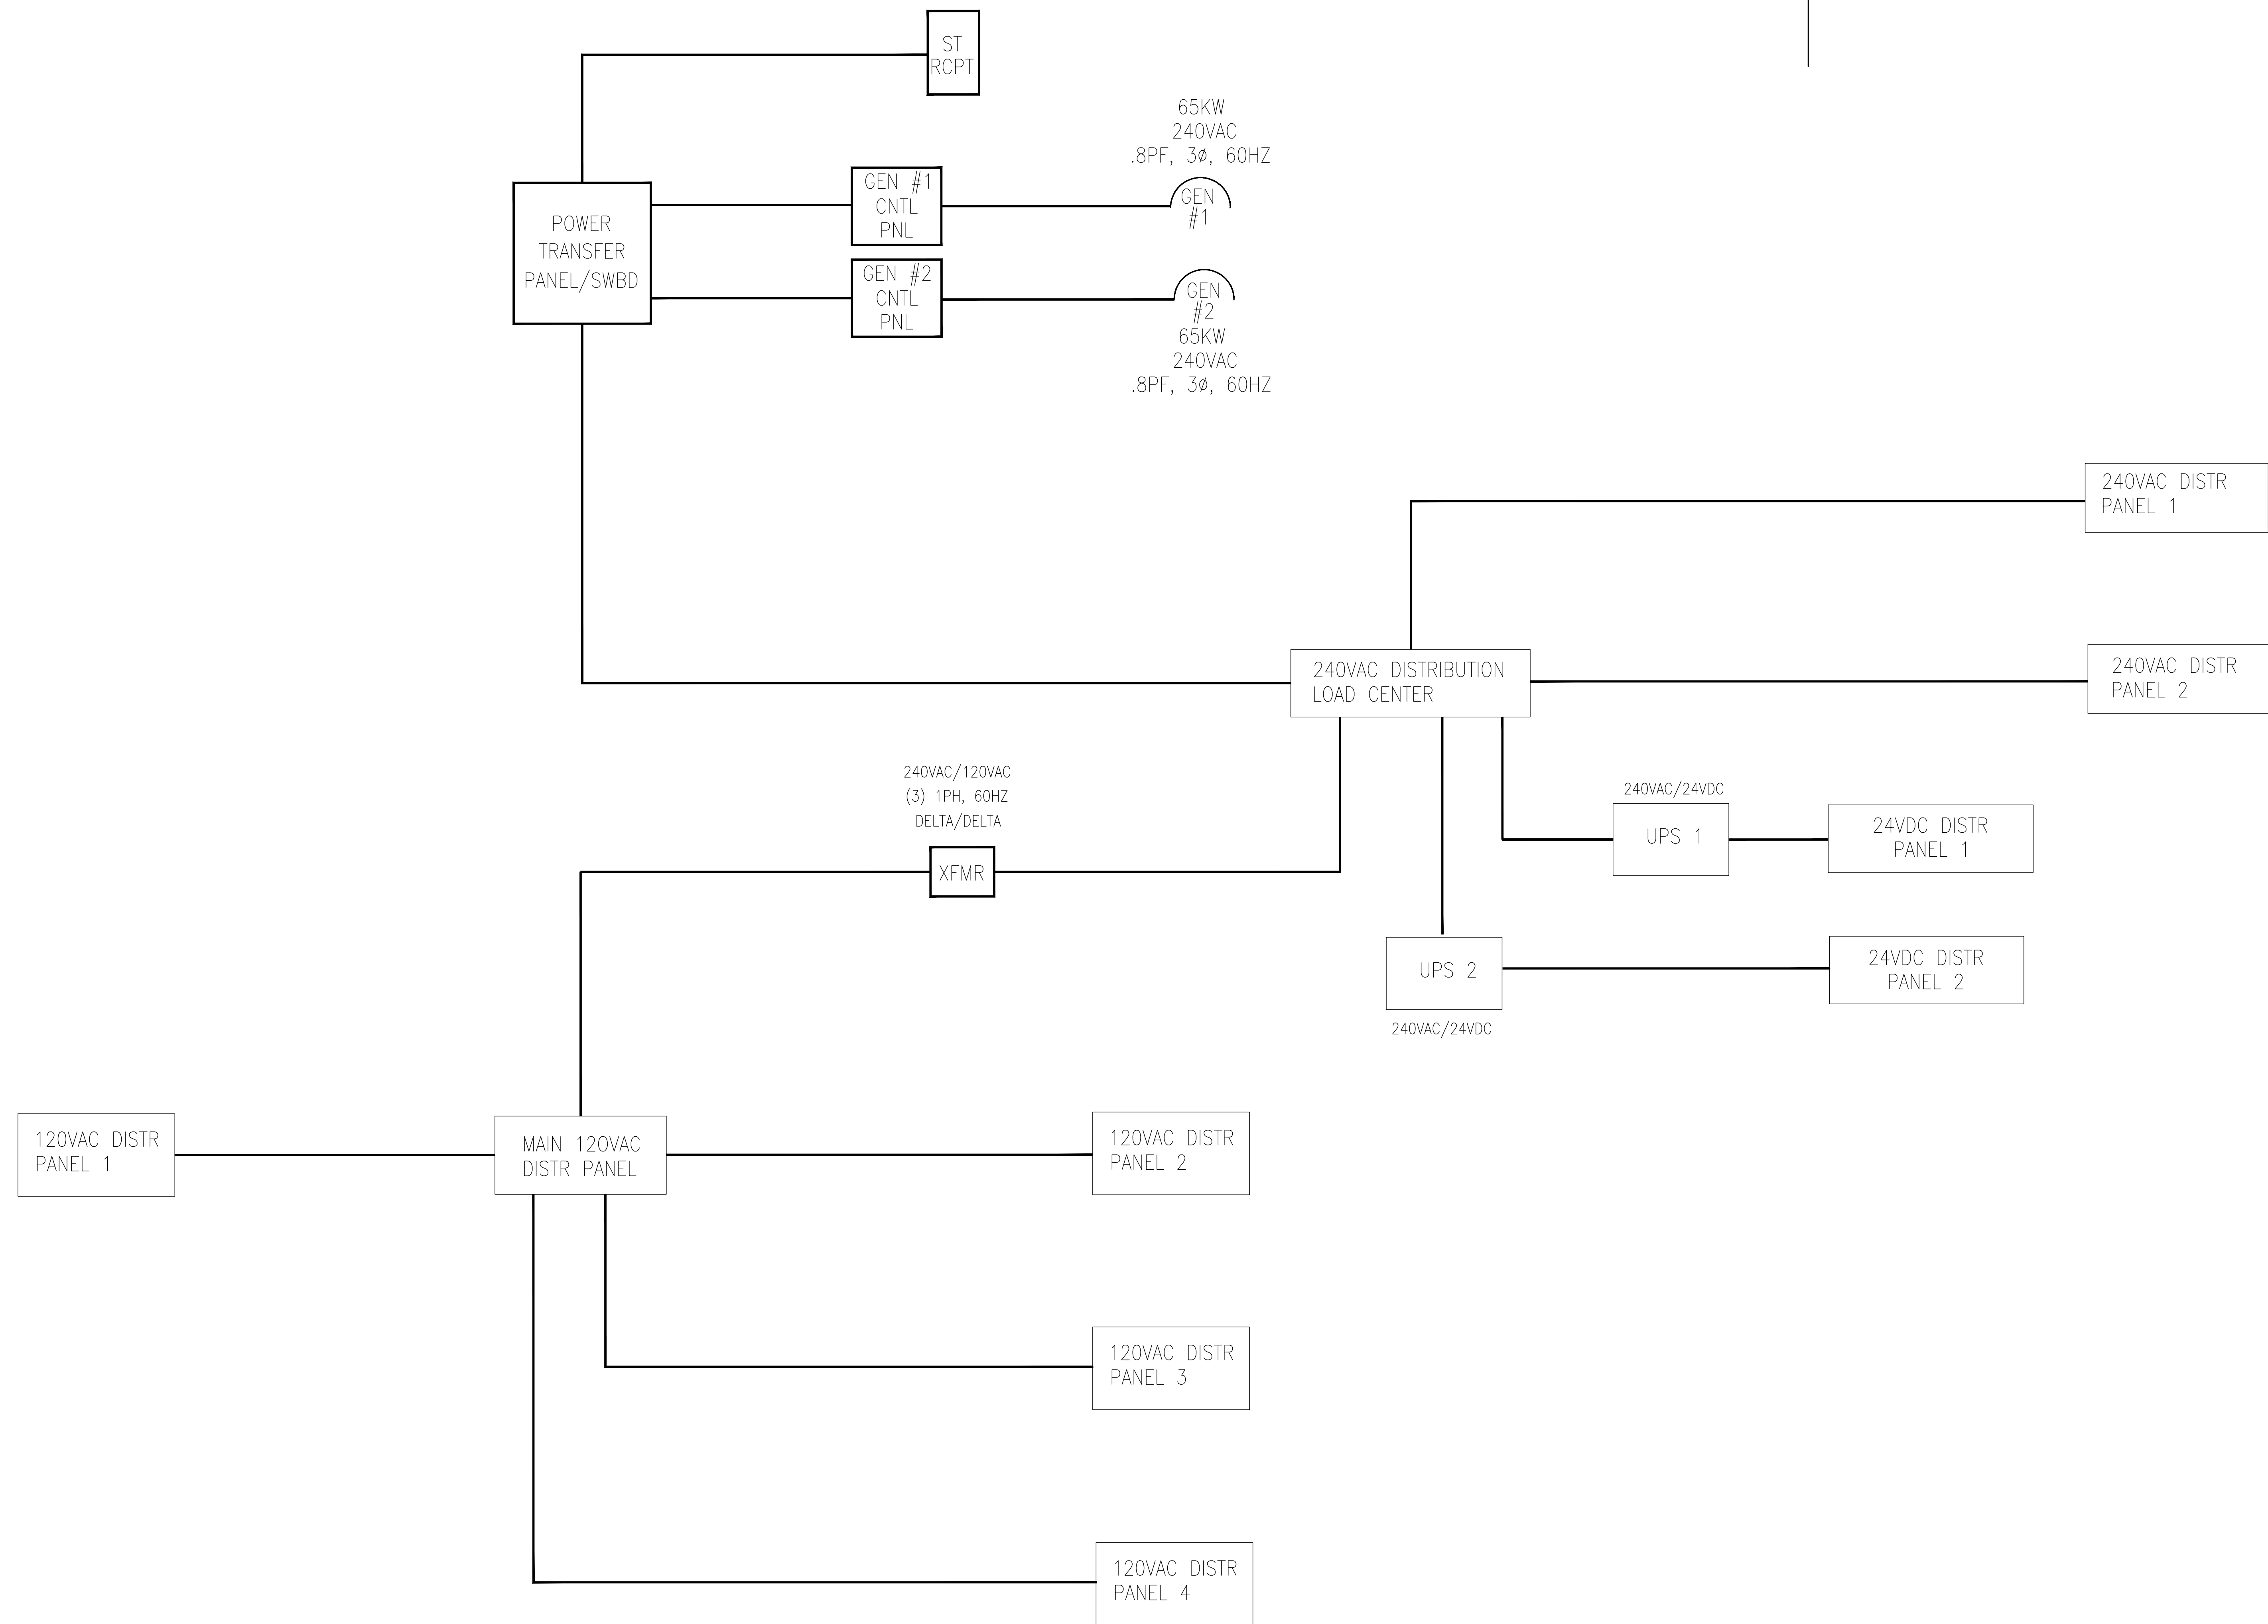


GENERAL NOTES

REVISIONS					DESCRIPTION	DATE	APPR. SIG & ORG
REV	SH	ZONE	ITEM				
0	-	-	-	PRELIMINARY RELEASE FOR DRAFT RFP	02/24/26		
1	-				-		
NO.	TITLE				DRAWING NO.		
REFERENCE PLANS							
SPECIAL NOTATIONS							
PRELIMINARY DRAWING ISSUED TO SUPPORT DRAFT RFP. DRAWING IS UNDER DEVELOPMENT, AND NOT APPROVED.							
RESERVATIONS:							
STINFO DESIGNATION							
DISTRIBUTION STATEMENT A: APPROVED FOR PUBLIC RELEASE. DISTRIBUTION IS UNLIMITED.							
		UNITED STATES COAST GUARD WASHINGTON, D.C. 20593					
		OFFICE OF NAVAL ENGINEERING					
		69 FT		HSC			
		HOMELAND SECURITY CUTTER LIGHT ELECTRICAL BLOCK DIAGRAM					
		TITLE SHEET & SYSTEM ARCHITECTURE					
DESIGNED: DSGN SIG /s/ MM/DD/YY		***SELECTED RECORD DRAWING***					
DRAWN: DRWN SIG /s/ MM/DD/YY		UPDATE REQUIRED FOR ALL AUTHORIZED CONFIGURATION CHANGES.					
CHECKED: CHKD SIG /s/ MM/DD/YY		SIZE		CAGE CODE		USCG DRAWING NO.	
APPROVED: APVD SIG /s/ MM/DD/YY		H		81340		69-HSCL-320-001	
USCG APPROVAL		SCALE: NONE		SHEET: 1 OF		REV 0	
APPR. AUTH							