

		8		7		6		5		4		3		2		1				
H	MATERIALS LIST										GENERAL NOTES				REVISIONS					
	REV	PC#	QTY	UNIT	MFR PART NO / NSN		DESCRIPTION		MATERIAL		REV				SH	ZONE	ITEM	DESCRIPTION	DATE	APPLV SIG & ORG
	0	1	AR	-	-		PLATE, 7.65#		STEEL		0				-	-	-	PRELIMINARY RELEASE FOR DRAFT RFP	02/24/26	
	0	2	AR	-	-		PLATE, 10.2#		STEEL		1. THE PURPOSE OF THIS DRAWING IS TO PROVIDE CONSTRUCTION INFORMATION AND MATERIAL NECESSARY FOR THE STRUCTURAL BULKHEADS AND DECK PLATING AND FRAMING OF THE USCG HSCL. 2. STRUCTURE SHOWN IS PRELIMINARY AND NOT FOR PRODUCTION. 3. SCANTLINGS REFLECT ABS MVR PART 3 AND ARE ABS GRADE H36 STEEL UNLESS OTHERWISE NOTED. 4. UNITS AND SIZES ARE US CUSTOMARY, DIMENSIONS ARE IN INCHES UNLESS OTHERWISE NOTED. 5. ALL SECTIONS ARE DRAWN LOOKING AFT UNLESS OTHERWISE NOTED.									
	0	3	AR	-	-		PLATE, 12.75#		STEEL											
	0	4	AR	-	-		PLATE, 20.4#		STEEL											
	0	5	AR	-	-		TEE, MT 3x2.2#		STEEL											
	0	6	AR	-	-		TEE, WT 8x10#		STEEL											
	0	7	AR	-	-		TEE, WT 6x7#		STEEL											
	0	8	AR	-	-		TEE, WT 5x6#		STEEL											
	0	9	AR	-	-		TEE, WT 7x11#		STEEL											
	0	10	AR	-	-		TEE, MT 4x3.25#		STEEL											
G																				
F																				
E																				
D																				
C																				
B																				
A																				

70

0

ELEVATIONS & DETAILS

60

0

1ST PLATFORM

50

0

SECTION VIEW OF BULKHEADS 43 & 49

40

0

SECTION VIEW OF BULKHEADS 4, 13, 26 & 33

30

0

WORKING DECK

20

0

MAIN DECK

10

0

TITLE SHEET & MATERIALS LIST

SH

REV

SHEET SUBTITLE

SHEET REVISION STATUS AND SUBTITLE INDEX

69-HSCL

ALL BOATS

ASSET CLASS

HULLS

APPLICABILITY

DESIGNED: DSGN SIG /s/ MM/DD/YY

DRAWN: DRWN SIG /s/ MM/DD/YY

CHECKED: CHKD SIG /s/ MM/DD/YY

APPROVED: APVD SIG /s/ MM/DD/YY

USCG APPROVAL

APPLV SIG /s/

APPLV AUTH

MM/DD/YY

MM/DD/YY

MM/DD/YY

MM/DD/YY

MM/DD/YY

MM/DD/YY

NONE

SIZE

DATE CODE

USCG DRAWING NO.

SCALE

SHEET: 1 OF 7

UPDATE REQUIRED FOR ALL AUTHORIZED CONFIGURATION CHANGES.

69-HSCL-101-002

0

UNITED STATES COAST GUARD

WASHINGTON, D.C. 20593

OFFICE OF NAVAL ENGINEERING

69 FT

HSCL

HOMELAND SECURITY CUTTER LIGHT

DECKS & BULKHEADS

TITLE SHEET & MATERIALS LIST

SELECTED RECORD DRAWING


UPDATE REQUIRED FOR ALL AUTHORIZED CONFIGURATION CHANGES.


69-HSCL-101-002


0

69-HSCL_101_002_0 Decks & Bulkheads.dwg

ELECTRONIC FILE NAME:

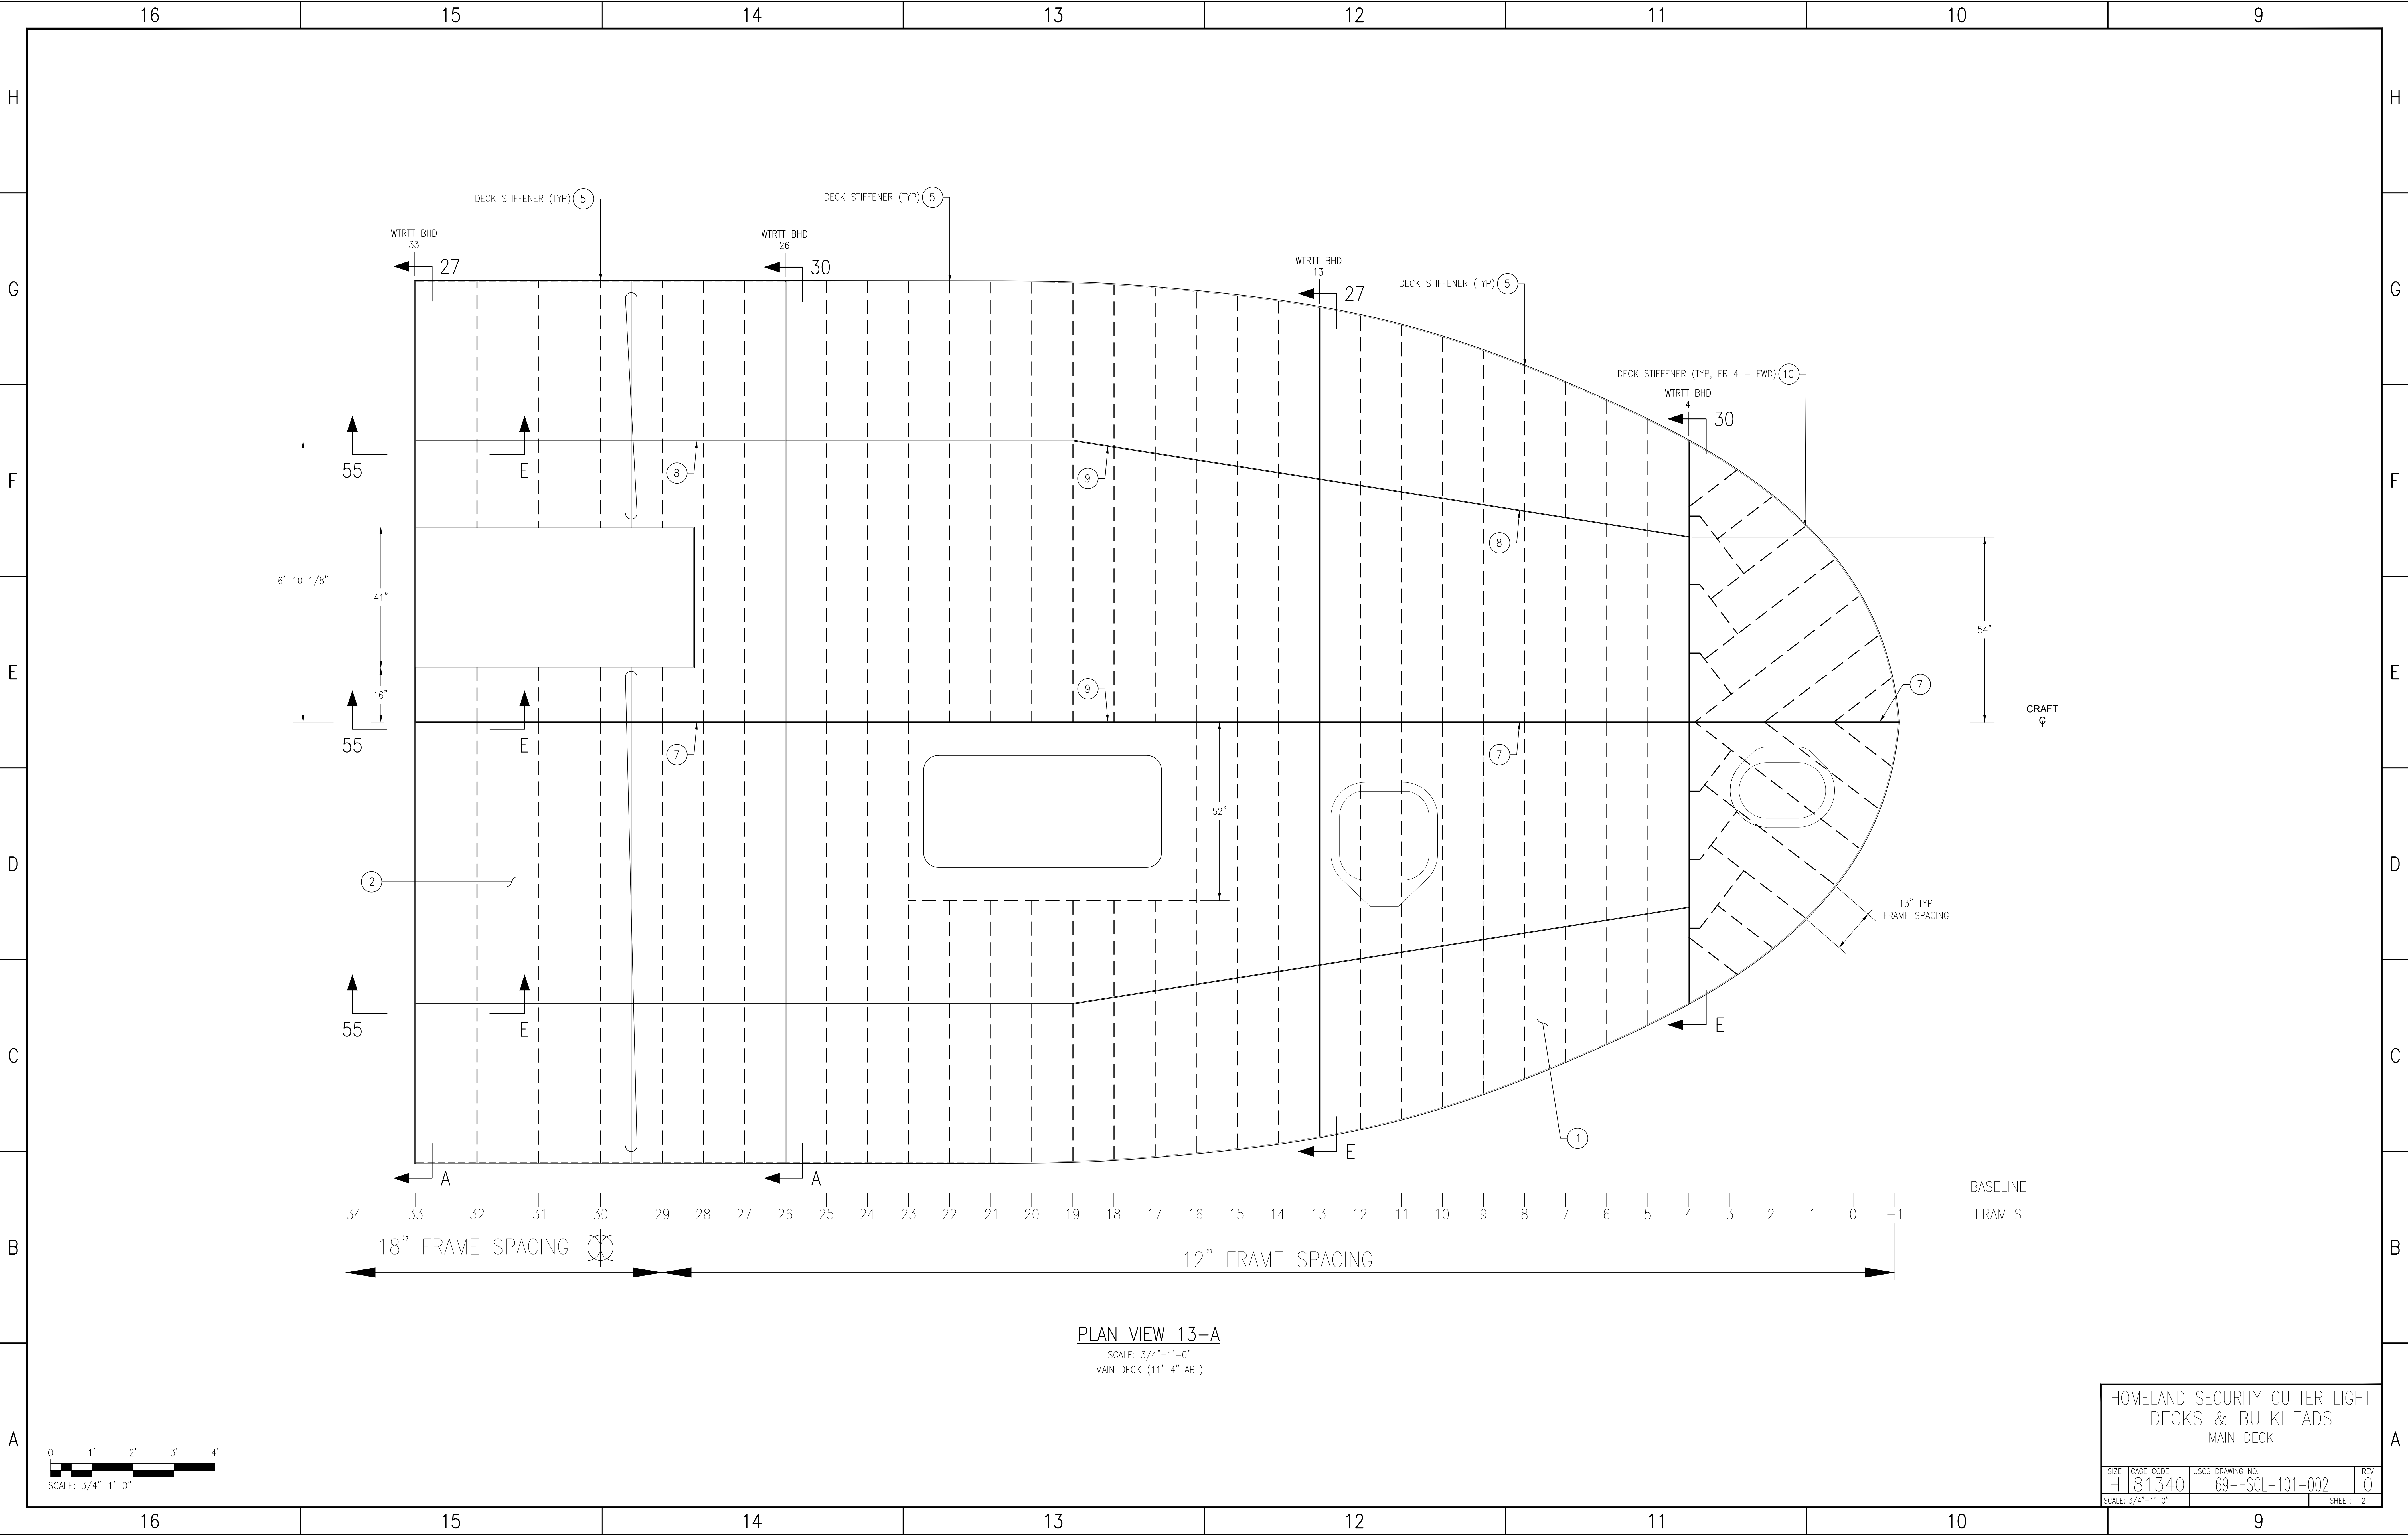

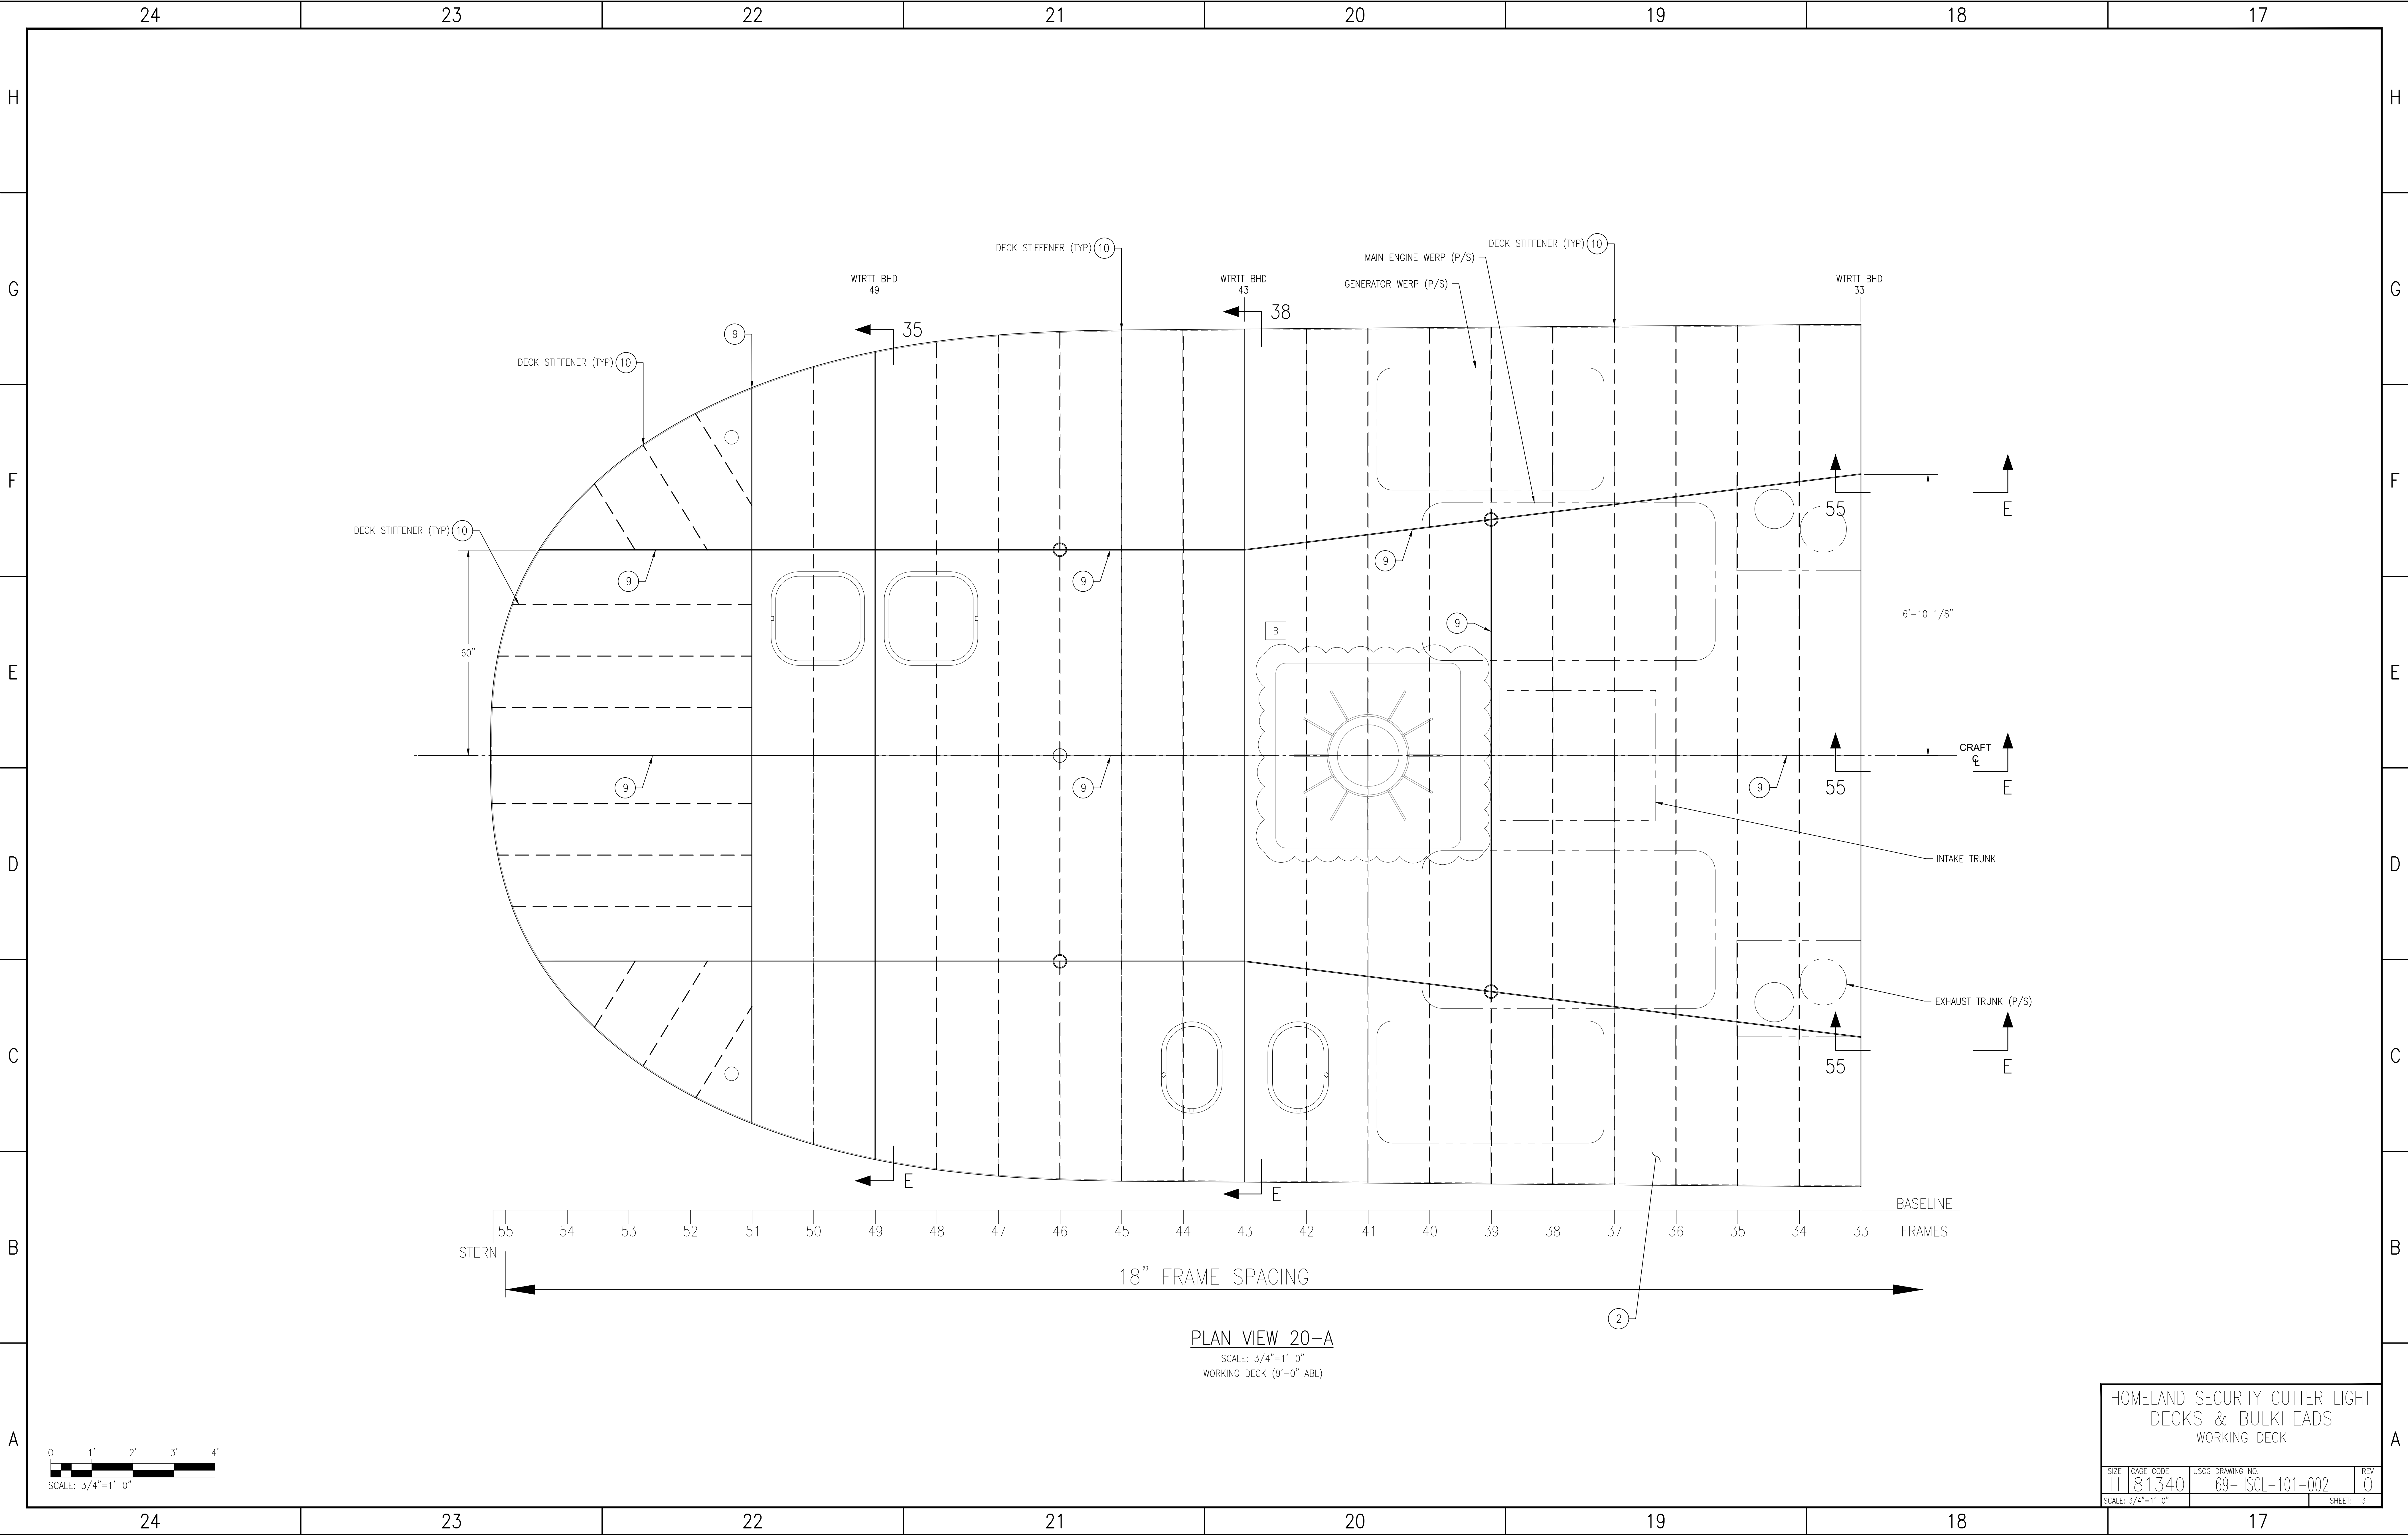

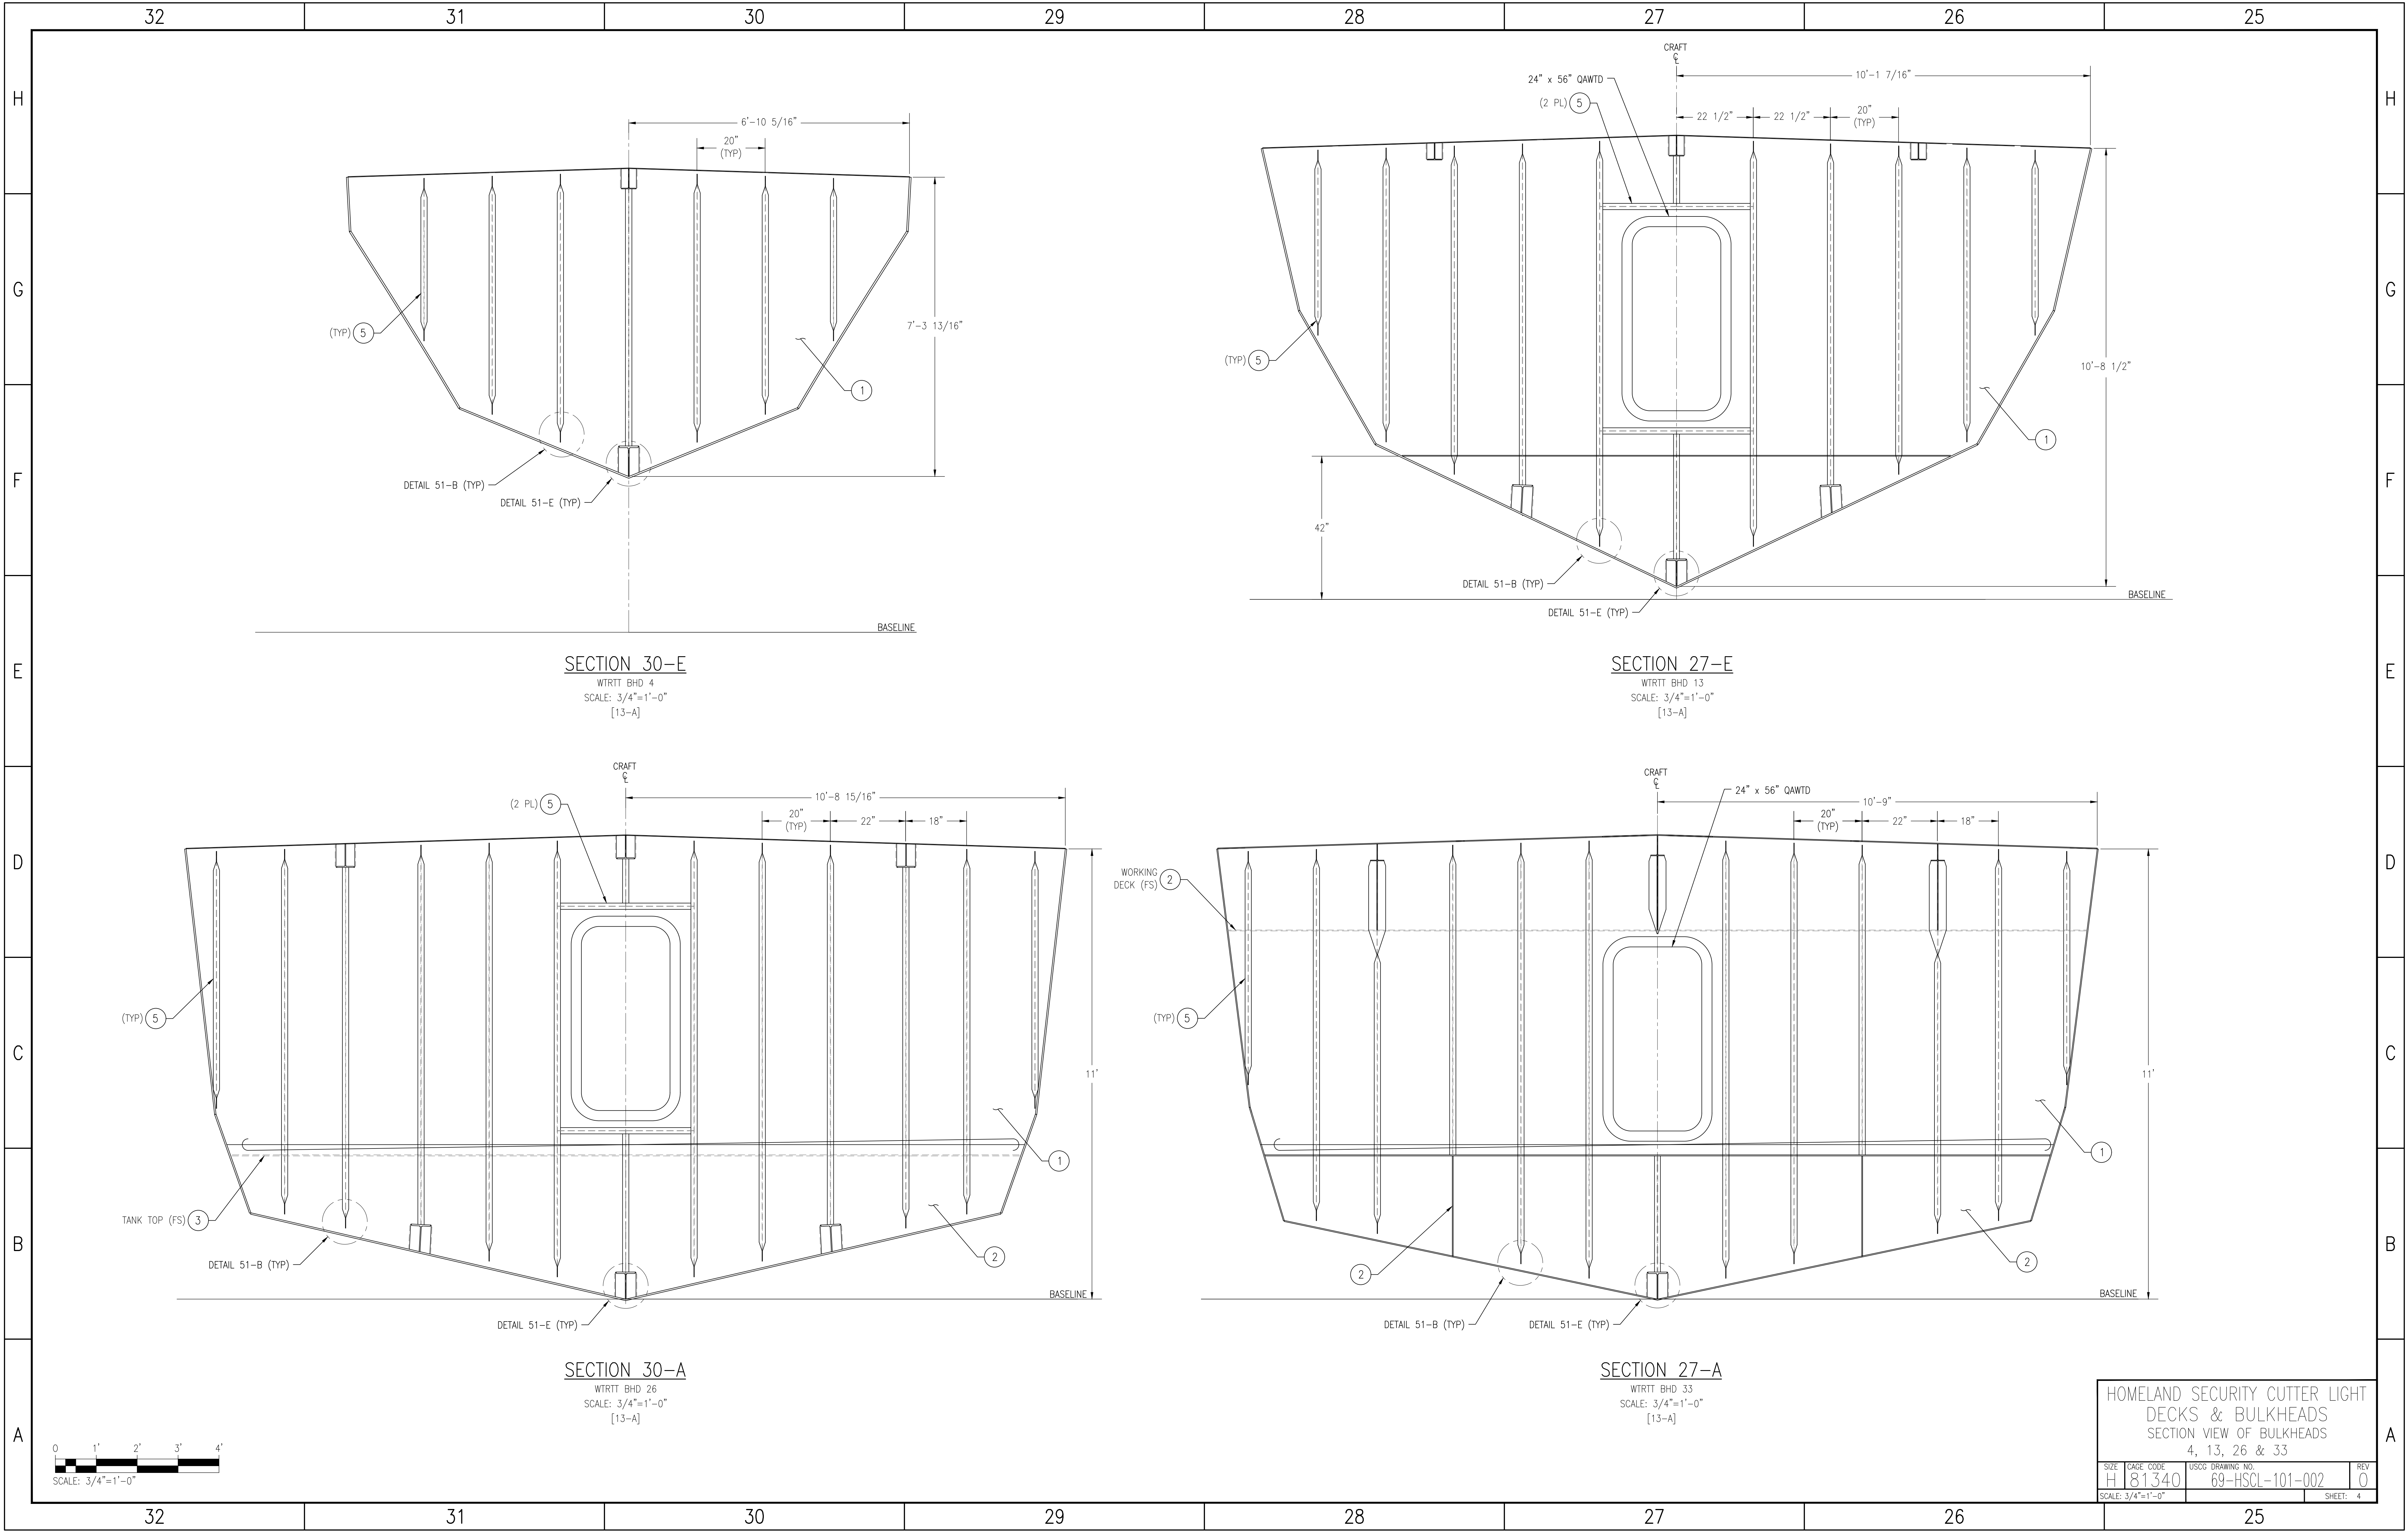

SECTION 30-E

WTRTT BHD 4
SCALE: 3/4"=1'-0"
[13-A]

SECTION 27-E

WTRTT BHD 13
SCALE: 3/4"=1'-0"
[13-A]

SECTION 30-A


WTRTT BHD 26
SCALE: 3/4"=1'-0"
[13-A]

SECTION 27-A




WTRTT BHD 33
SCALE: 3/4"=1'-0"
[13-A]

HOMELAND SECURITY CUTTER LIGHT
DECKS & BULKHEADS
SECTION VIEW OF BULKHEADS
4, 13, 26 & 33

SIZE	CAGE CODE	USCG DRAWING NO.	REV
H	181340	69-HSCL-101-002	0
SCALE: 3/4"=1'-0"			SHEET: 4

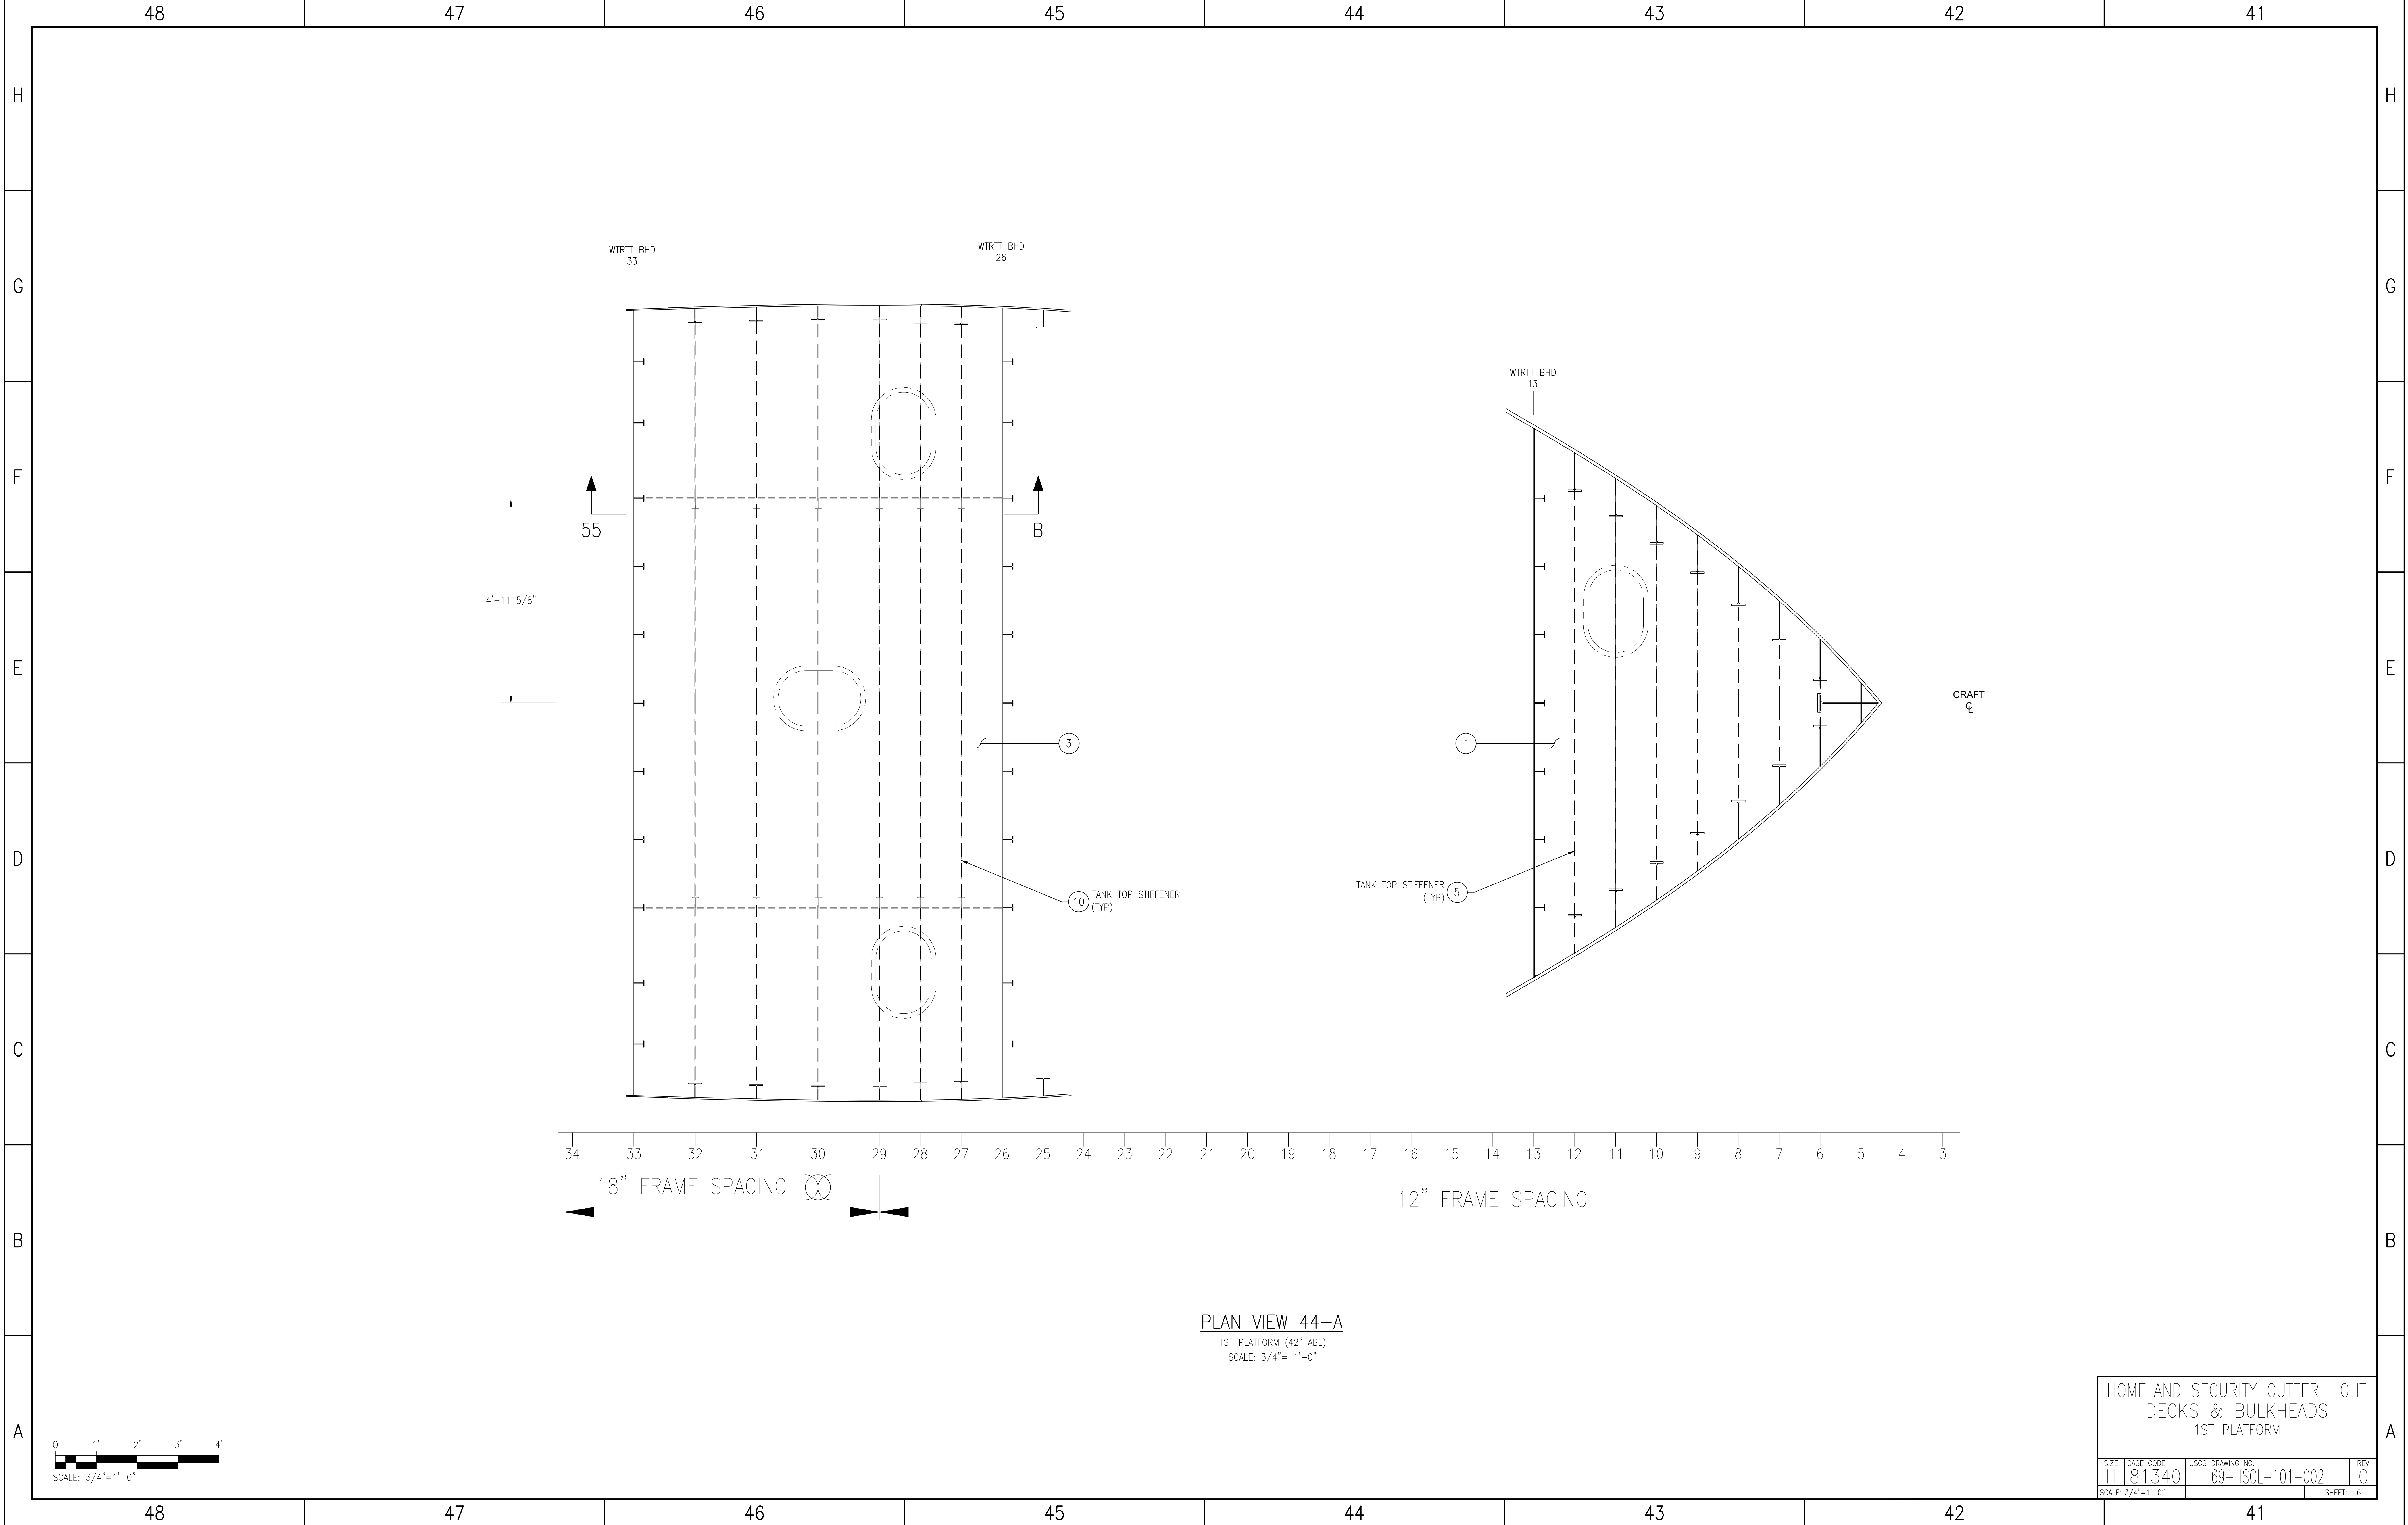

HOMELAND SECURITY CUTTER LIGHT DECKS & BULKHEADS 1ST PLATFORM			
SIZE	CAGE CODE	USCG DRAWING NO.	REV
H	81340	69-HSCL-101-002	0
SCALE: 3/4"=1'-0"		SHEET: 6	

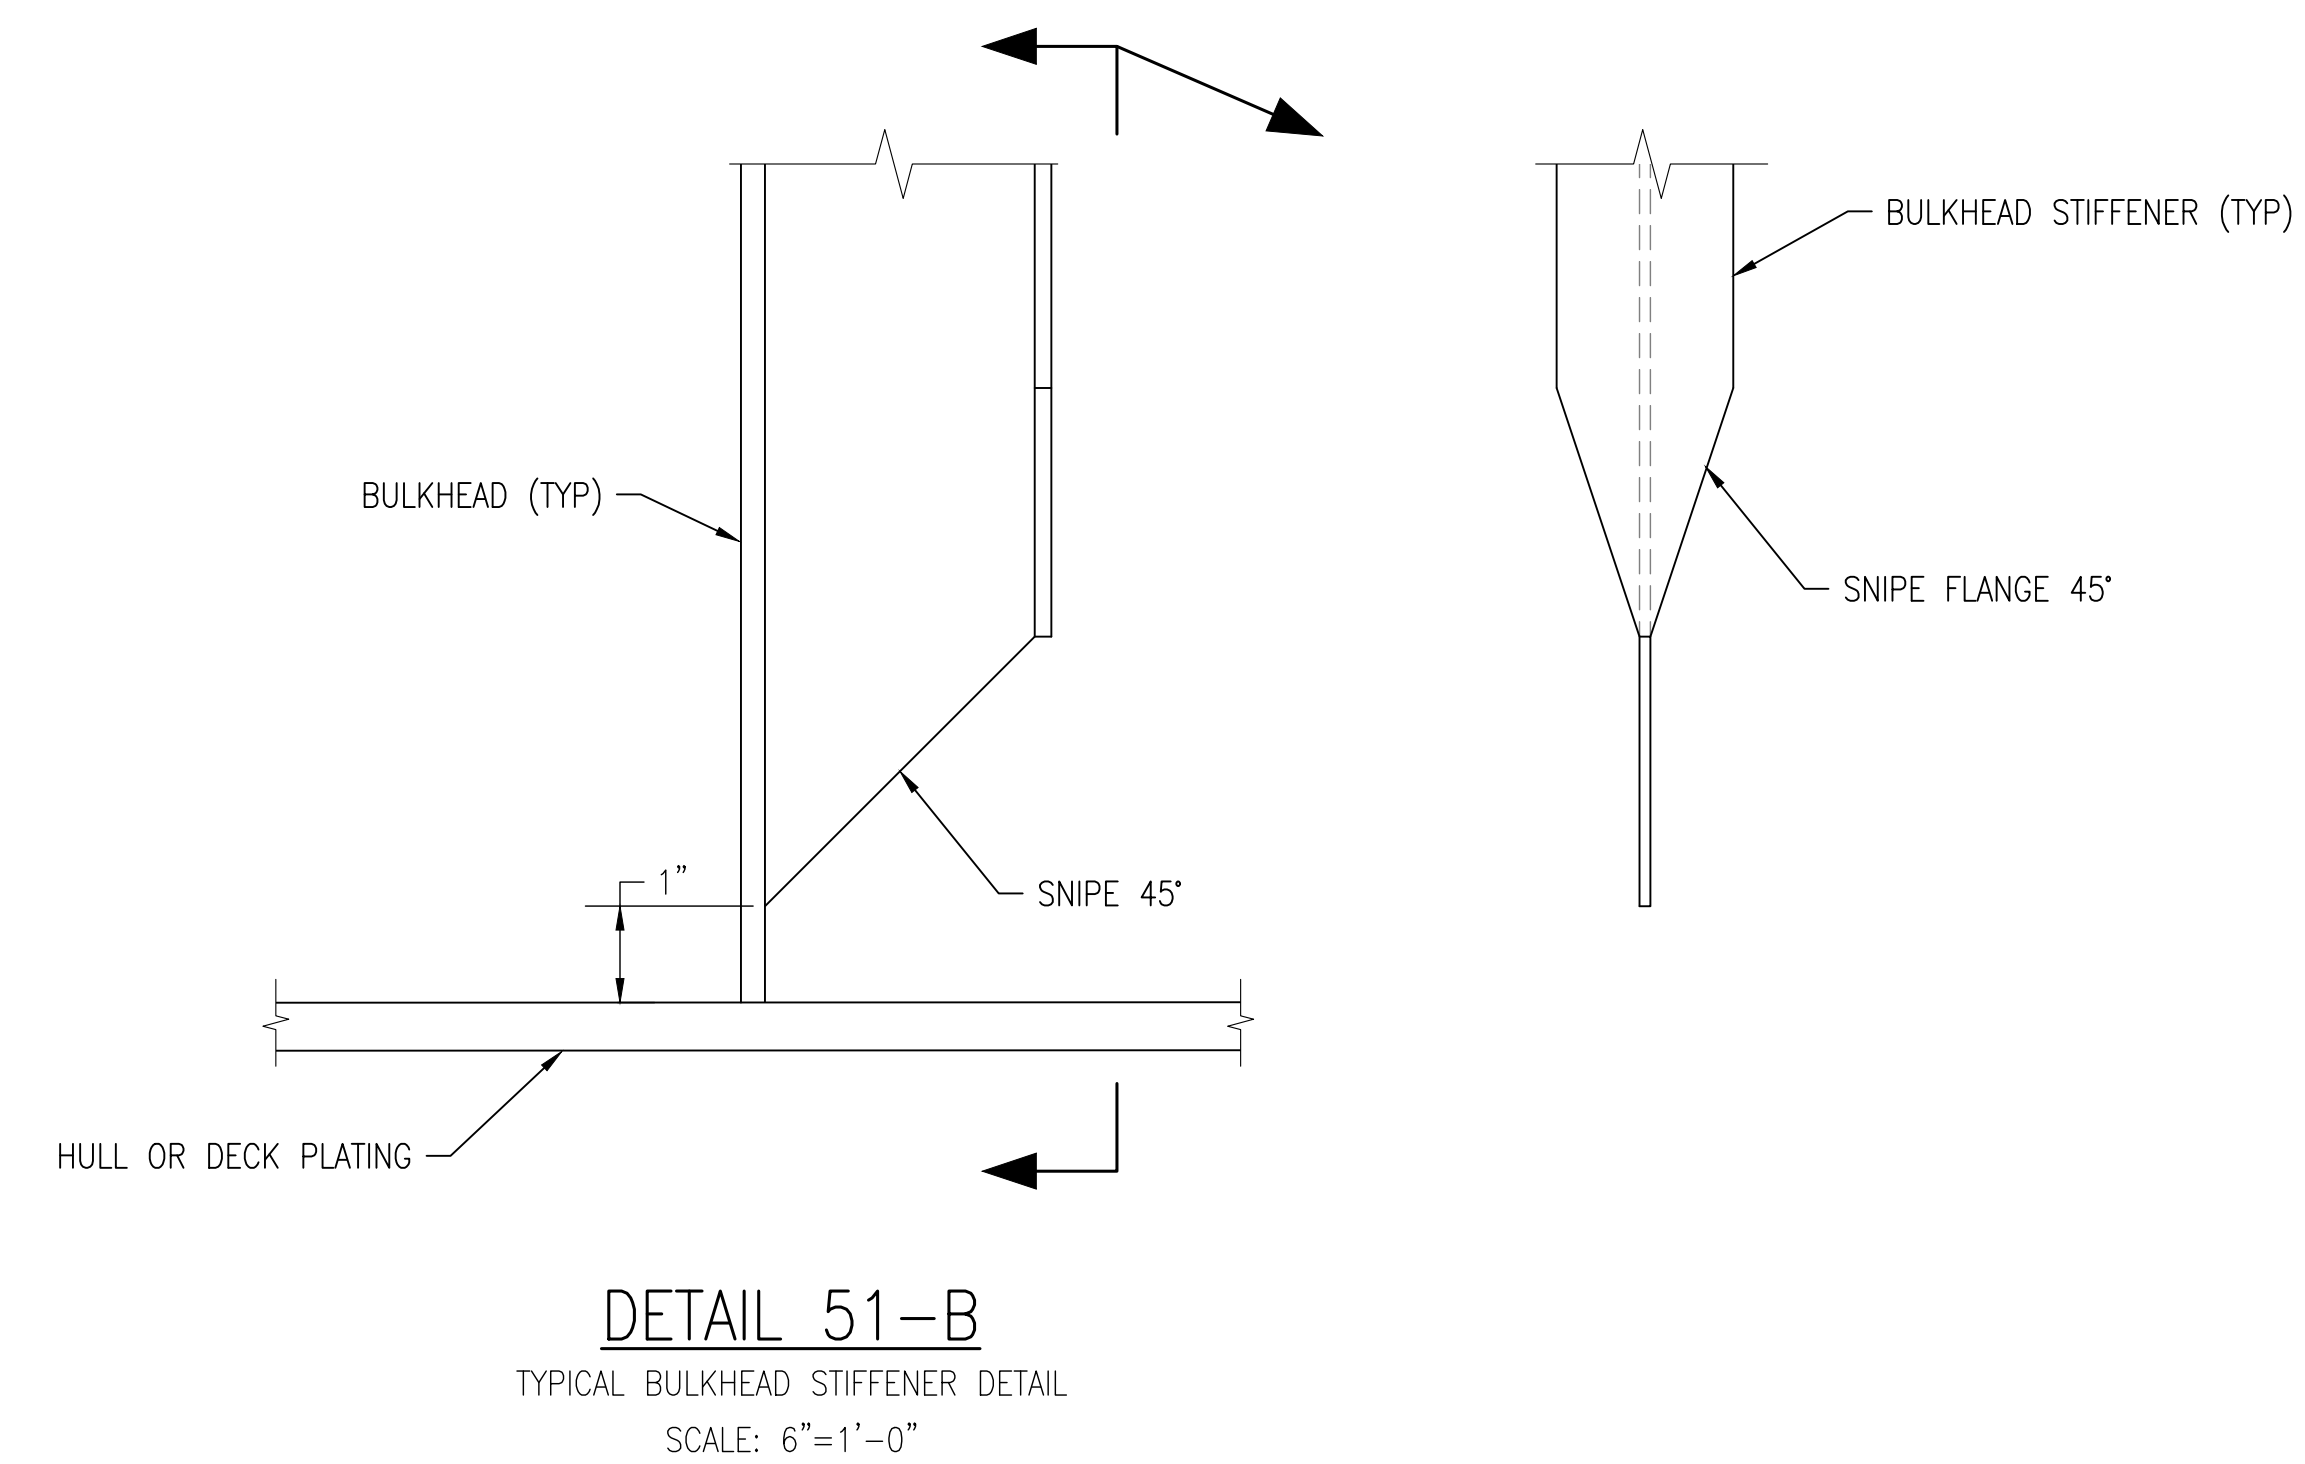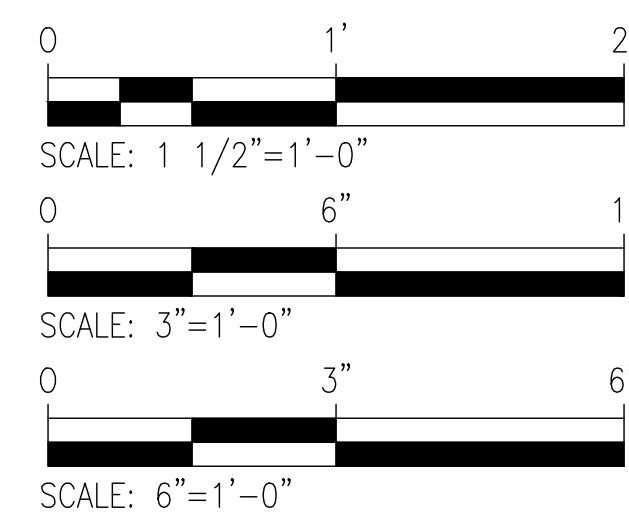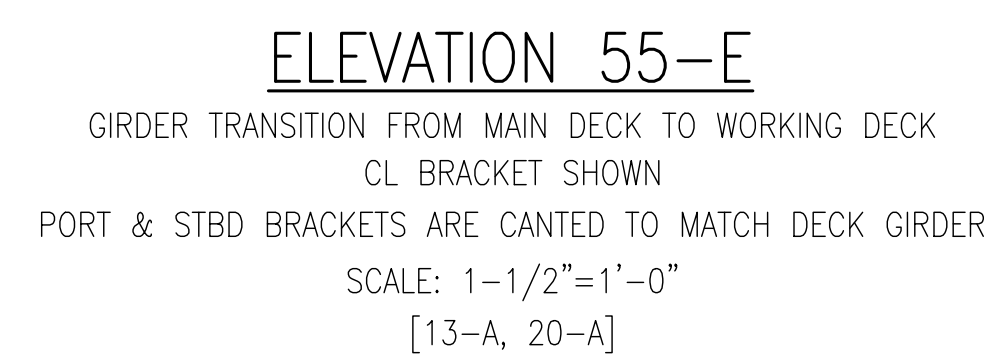

HOMELAND SECURITY CUTTER LIGHT DECKS & BULKHEADS ELEVATIONS & DETAILS				A
SIZE H	CAGE CODE 81340	USCG DRAWING NO. 69-HSC-101-002	REV 0	
SCALE: AS NOTED			SHEET: 7	