



FILE NAME: S:\projects\201\A\1416 - MIDANT CL 2nd MSOB Battalion HQ (P1219)\dwg\A2 COMPANY BUILDINGS\1416 A2-A-101.dwg LAYOUT NAME: A-101 PLOTTED: Friday, November 04, 2016 - 4:41pm

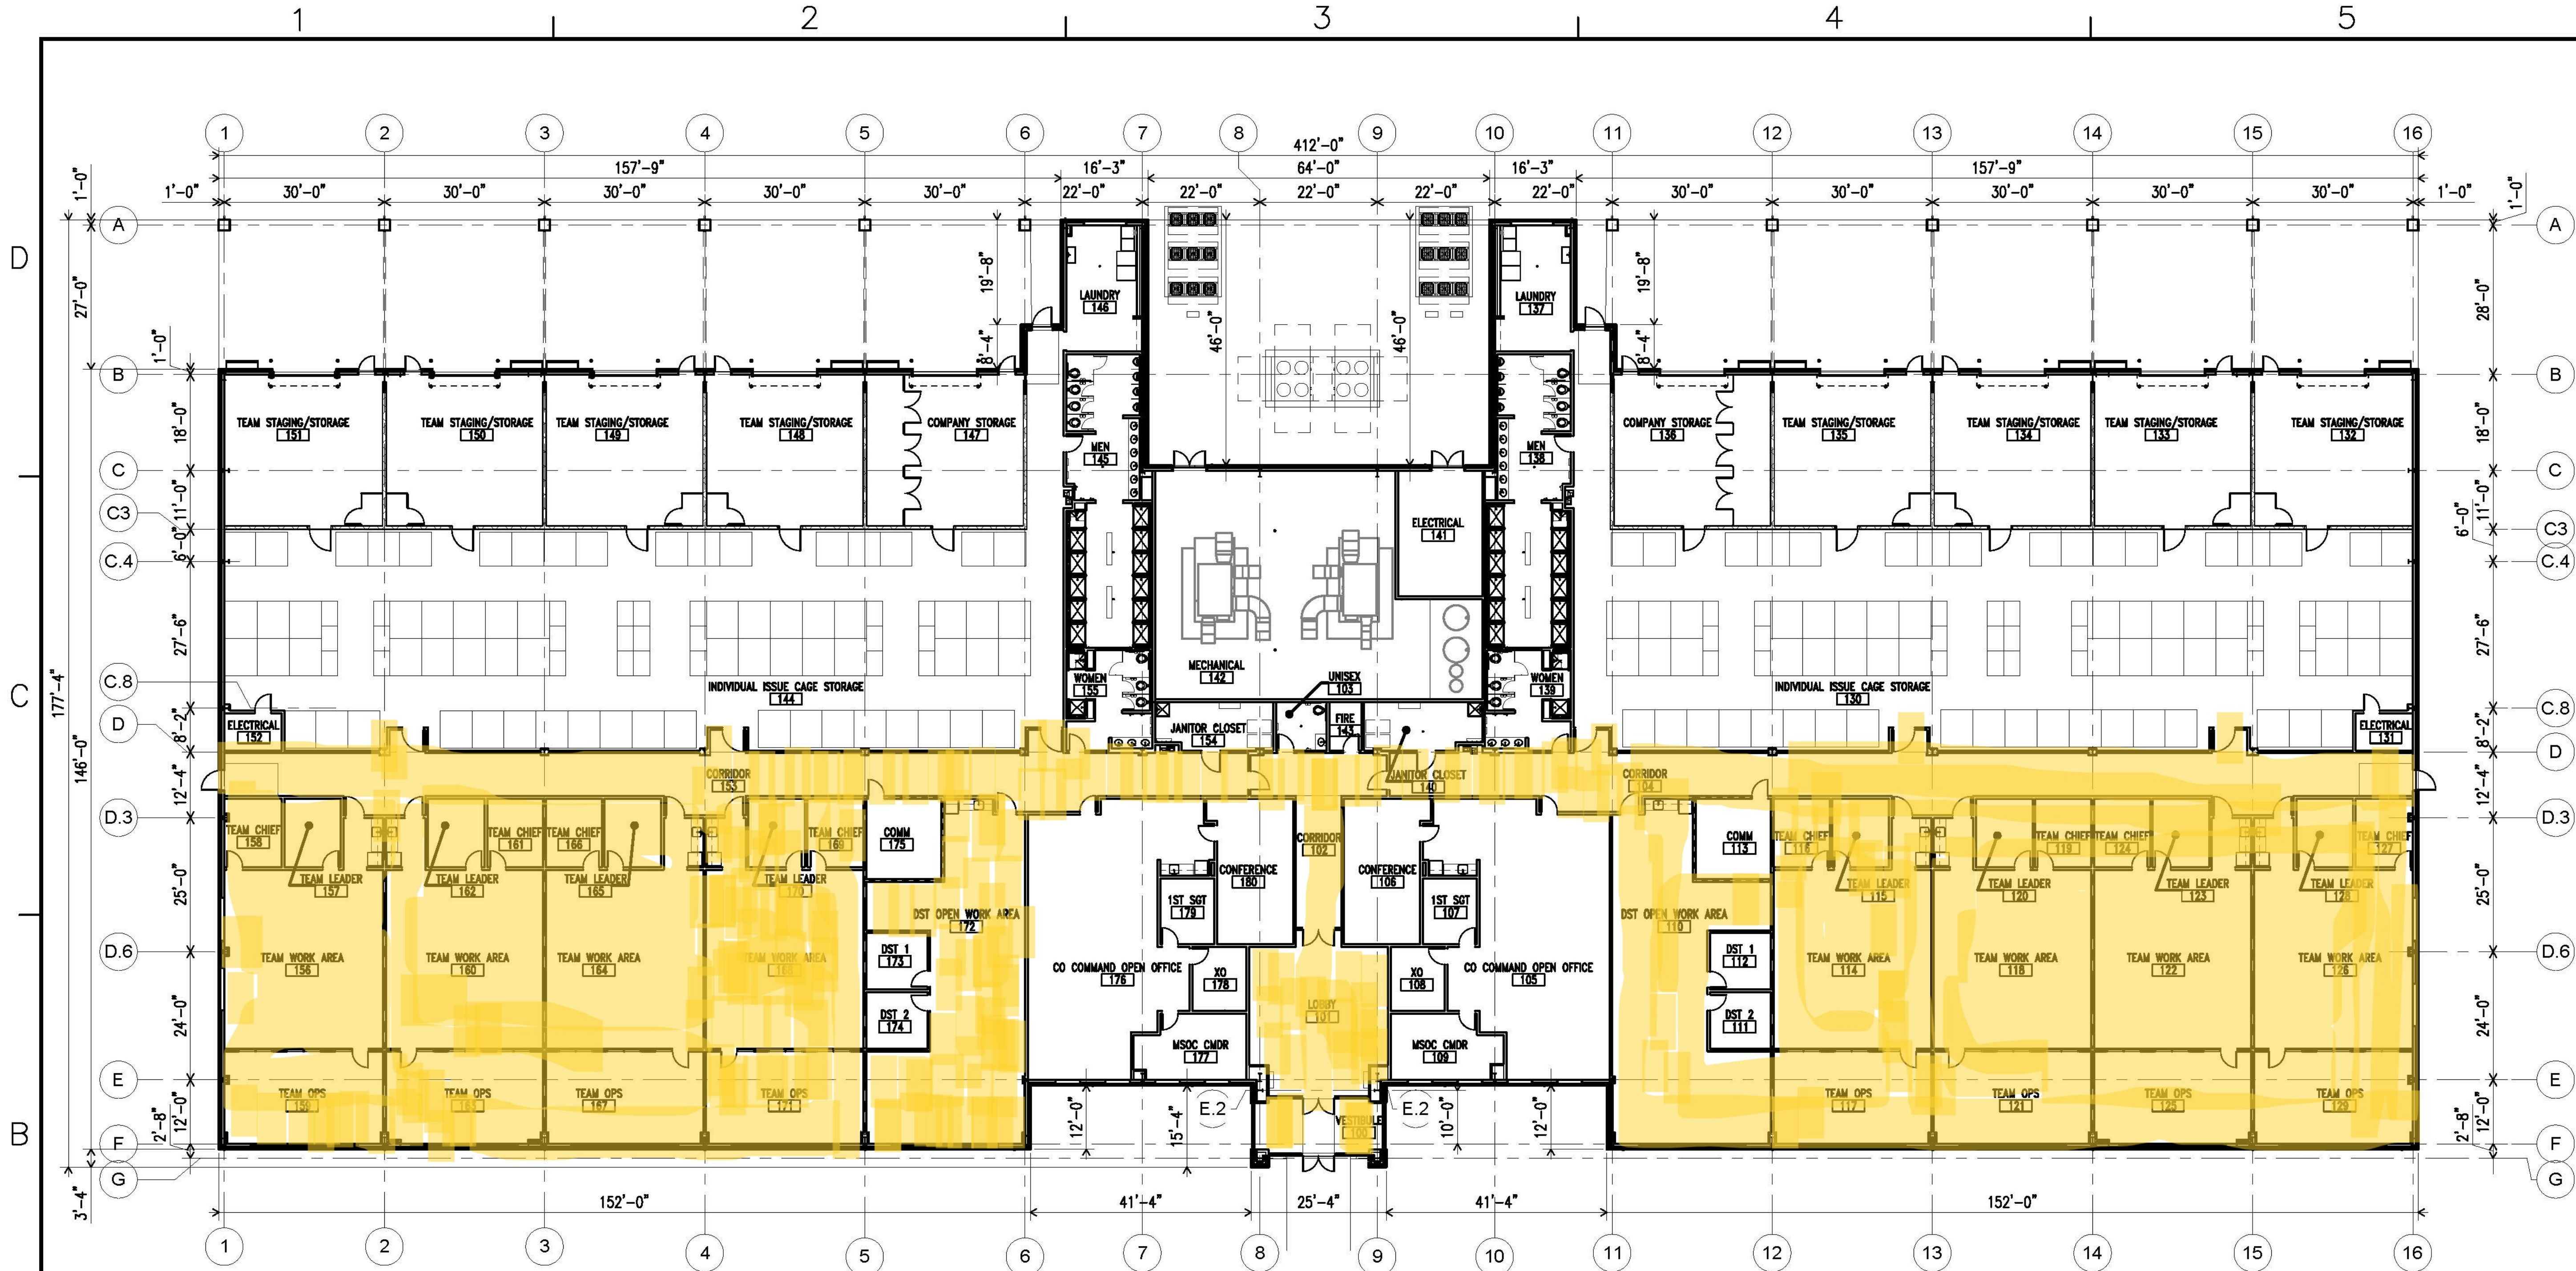

A3 COMPREHENSIVE FLOOR PLAN
SCALE: 1/16"=1'-0"



GENERAL CONSTRUCTION NOTES

1. BUILDINGS REPRESENT BOTH COMPANY BUILDINGS. SEE GENERAL NOTE 1 ON SHEET G-001
2. CLEARANCE AND MOUNTING STANDARDS FOR ACCESSIBILITY, SEE SHEETS A-520 AND A-521
3. FOR SYMBOL LEGEND, SEE SHEET G-003

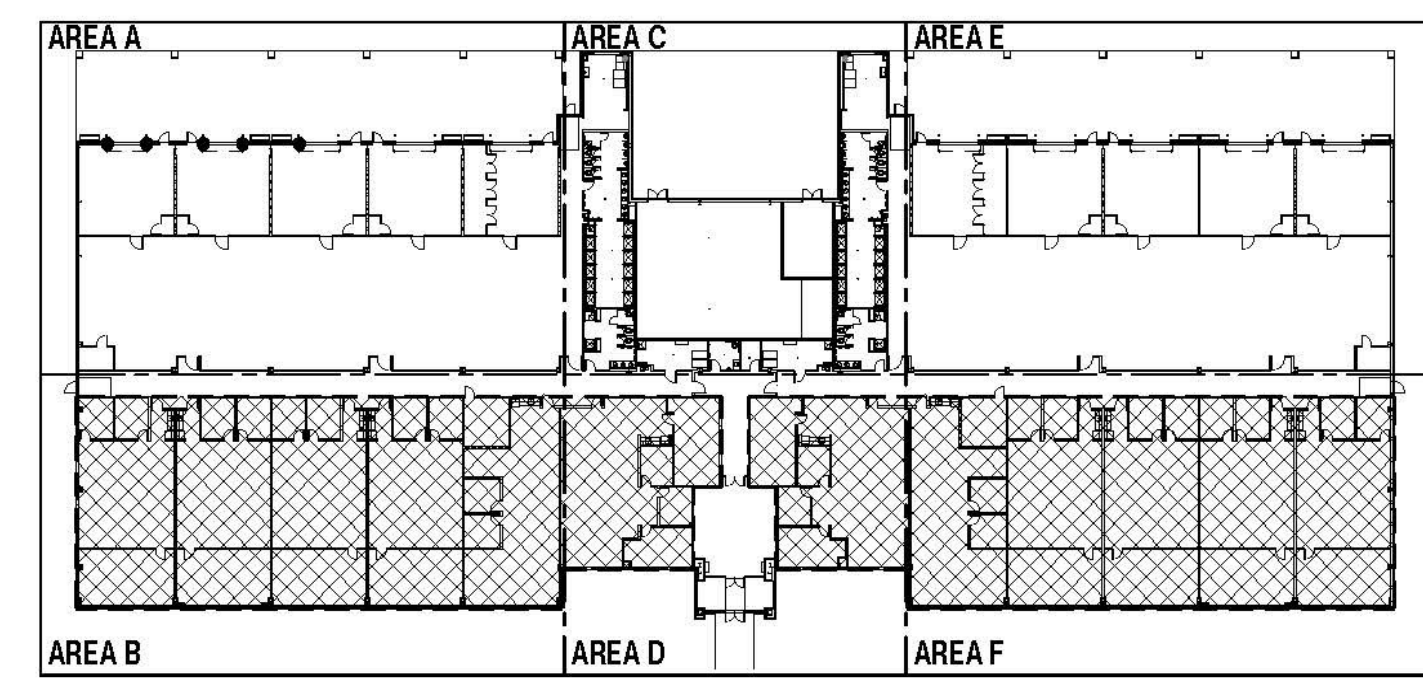

KEY PLAN

SCALE: 1"=60'

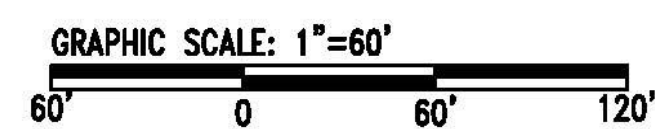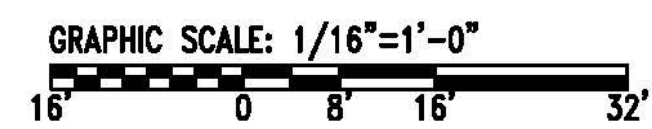

A2
CO BLDG
DRAWING NO. 12736574
SHEET 24 OF 234
A-101

DATE		APPR
DESCRIPTION		REV
NAVFAC		
GARDEN JOHNSON ENGINEERING		
REGISTERED ARCHITECT		
6640		
30-C Pollock Street, New Bern, NC 28550		
516.639.4333 mbfarchitects.com		
mbf architects pa		
30-C Pollock Street, New Bern, NC 28550		
516.639.4333 mbfarchitects.com		
APPROVED		
FOR COMMANDER NAVFAC		
ACTIVITY		
SATISFACTORY TO DATE		
DES REL / REL / ASM / CH / DUE / REL		
PW / SM		
BRANCH MANAGER		
CHIEF ENG / ARCH		
FIRE PROTECTION		
NAVAL FACILITIES ENGINEERING COMMAND		
NAVAL FACILITIES ENGINEERING COMMAND ~ MIDATLANTIC		
LAFAYETTE COMPLEX, NORFOLK, VA		
BPT MARINE CORPS		
MARINE CORPS BASE		
CAMP LEJEUNE, NC		
SOF MARINE BATTALION		
COMPANY/TEAM FACILITIES - P1219		
SOF COMBAT SERVICE SUPPORT FACILITY - P1288		
COMPREHENSIVE FLOOR PLAN		
SCALE: AS NOTED		
PROJECT NO.: G114417		
CONSTR. CONTR. NO.		
NAVFAC DRAWING NO.		
12736574		
SHEET 24 OF 234		
A-101		
DRAWING REVISION: 10 MARCH 2008		