


11/20/2025 8:36:13 AM
C:\Users\Brian.Pacansky\Documents\B\DOCS\1075-1625040-E_Brian.Pacansky\QDKV\EL104

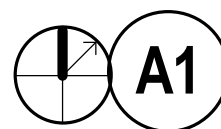

SECOND FLOOR PLAN AREA B - LIGHTING

1/8" = 1'-0"




GENERAL SHEET NOTES

SHEET KEYNOTES

- SUSPEND P3A FIXTURES IN THIS ROOM AT 25' AFF, UON.
- TO LIGHT FIXTURES ON FIRST FLOOR.

KEY PLAN

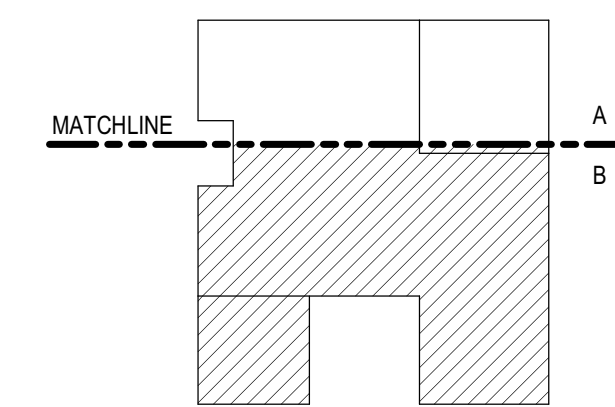

GRAPHIC SCALE(S)



DATE	SYMBOL	DESCRIPTION
11/21/25	1	CONSOLIDATED REVISIONS

APPROVED	FOR COMMANDER NAVFAC
ACTIVITY	Approved by Don Bryant, PE, N10 Facilities Engineer, NSWDG via Email
SATISFACTORY TO DATE	07/09/2025
DES	BSP
DRW	MSW
CHK	SPS
PMIDM	JT/SW
BRANCH MANAGER	WRB
CHIEF ENGINEER	JWJ
FIRE PROTECTION	HPN

DEPARTMENT OF THE NAVY	NAVAL FACILITIES ENGINEERING SYSTEMS COMMAND
NAVAL FACILITIES ENGINEERING SYSTEMS COMMAND - MID-ATLANTIC	NAVAL STATION - NORFOLK, VA
NAS OCEANA, DAM NECK ANNEX	Q-1075 SOF OPERATIONS BUILDING ADDITION
SECOND FLOOR PLAN AREA B - LIGHTING	

SCALE: AS NOTED
PROJECT NO.: 1625040
CONSTR. CONTR. NO. N40085-19-D-9041
NAVFAC DRAWING NO. 12929083
SHEET 178 OF 239

EL104



CLARKNEXSEN
A JMET Company
4525 MAIN STREET
SUITE 1400
VIRGINIA BEACH, VA 23462
757-455-5800 FAX 757-455-5638
WWW.CLARKNEXSEN.COM

APPROVED
FOR COMMANDER NAVFAC
ACTIVITY
Approved by Don Bryant, PE, N10
Facilities Engineer, NSWDG
via Email
SATISFACTORY TO DATE 07/09/2025
DES BSP DRW MSW CHK SPS
PMIDM JT/SW
BRANCH MANAGER WRB
CHIEF ENGINEER JWJ
FIRE PROTECTION HPN

DEPARTMENT OF THE NAVY
NAVAL FACILITIES ENGINEERING SYSTEMS COMMAND
NAVAL FACILITIES ENGINEERING SYSTEMS COMMAND - MID-ATLANTIC
NAVAL STATION - NORFOLK, VA
NAS OCEANA, DAM NECK ANNEX
Q-1075 SOF OPERATIONS BUILDING ADDITION
SECOND FLOOR PLAN AREA B - LIGHTING

SCALE: AS NOTED
PROJECT NO.: 1625040
CONSTR. CONTR. NO. N40085-19-D-9041
NAVFAC DRAWING NO. 12929083
SHEET 178 OF 239

EL104

DRAWING REVISION: 25 AUGUST 2020

1

2

3

UNCLASSIFIED

4

5

GENERAL SHEET NOTES

SHEET KEYNOTES

- 1 REUSE JUNCTION BOX ABANDONED DURING DEMOLITION OF EXISTING RECEPTACLE. PROVIDE EXTENSION RING.




CLARKNEXSEN
4525 MAIN STREET
SUITE 1400
VIRGINIA BEACH, VA 23462
757-455-5800 FAX 757-455-5638
WWW.CLARKNEXSEN.COM

FOR COMMANDER NAVFAC
ACTIVITY Approved by Don Bryant, PE, N10
Facilities Engineer, NSWDG
via Email
SATISFACTORY TO DATE 07/09/2025
DES BSP DRW MSW CHK SPS
PMDM JT/SV
BRANCH MANAGER WRB
CHIEF ENGINEER JWJ
FIRE PROTECTION HPN



DEPARTMENT OF THE NAVY
NAVAL FACILITIES ENGINEERING SYSTEMS COMMAND
NAVAL FACILITIES ENGINEERING SYSTEMS COMMAND - MID-ATLANTIC
NAVAL STATION - NORFOLK, VA
NAS OCEANA, DAM NECK ANNEX
Q-1075 SOF OPERATIONS BUILDING ADDITION

SCALE: AS NOTED
EPROJECT NO.: 1625040
CONSTR. CONTR. NO. N40085-19-D-9041
NAVFAC DRAWING NO. 12929087
SHEET 182 OF 239
EP101

KEY PLAN

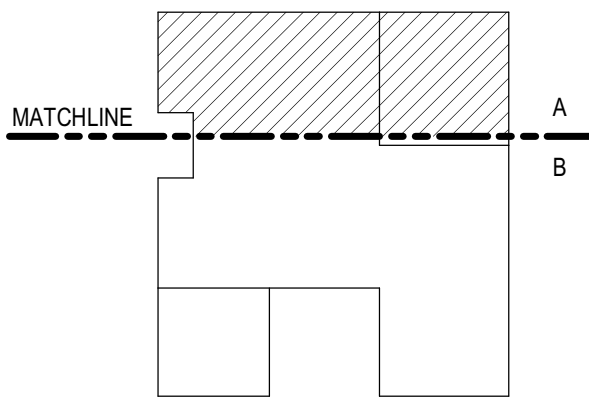

GRAPHIC SCALE(S)

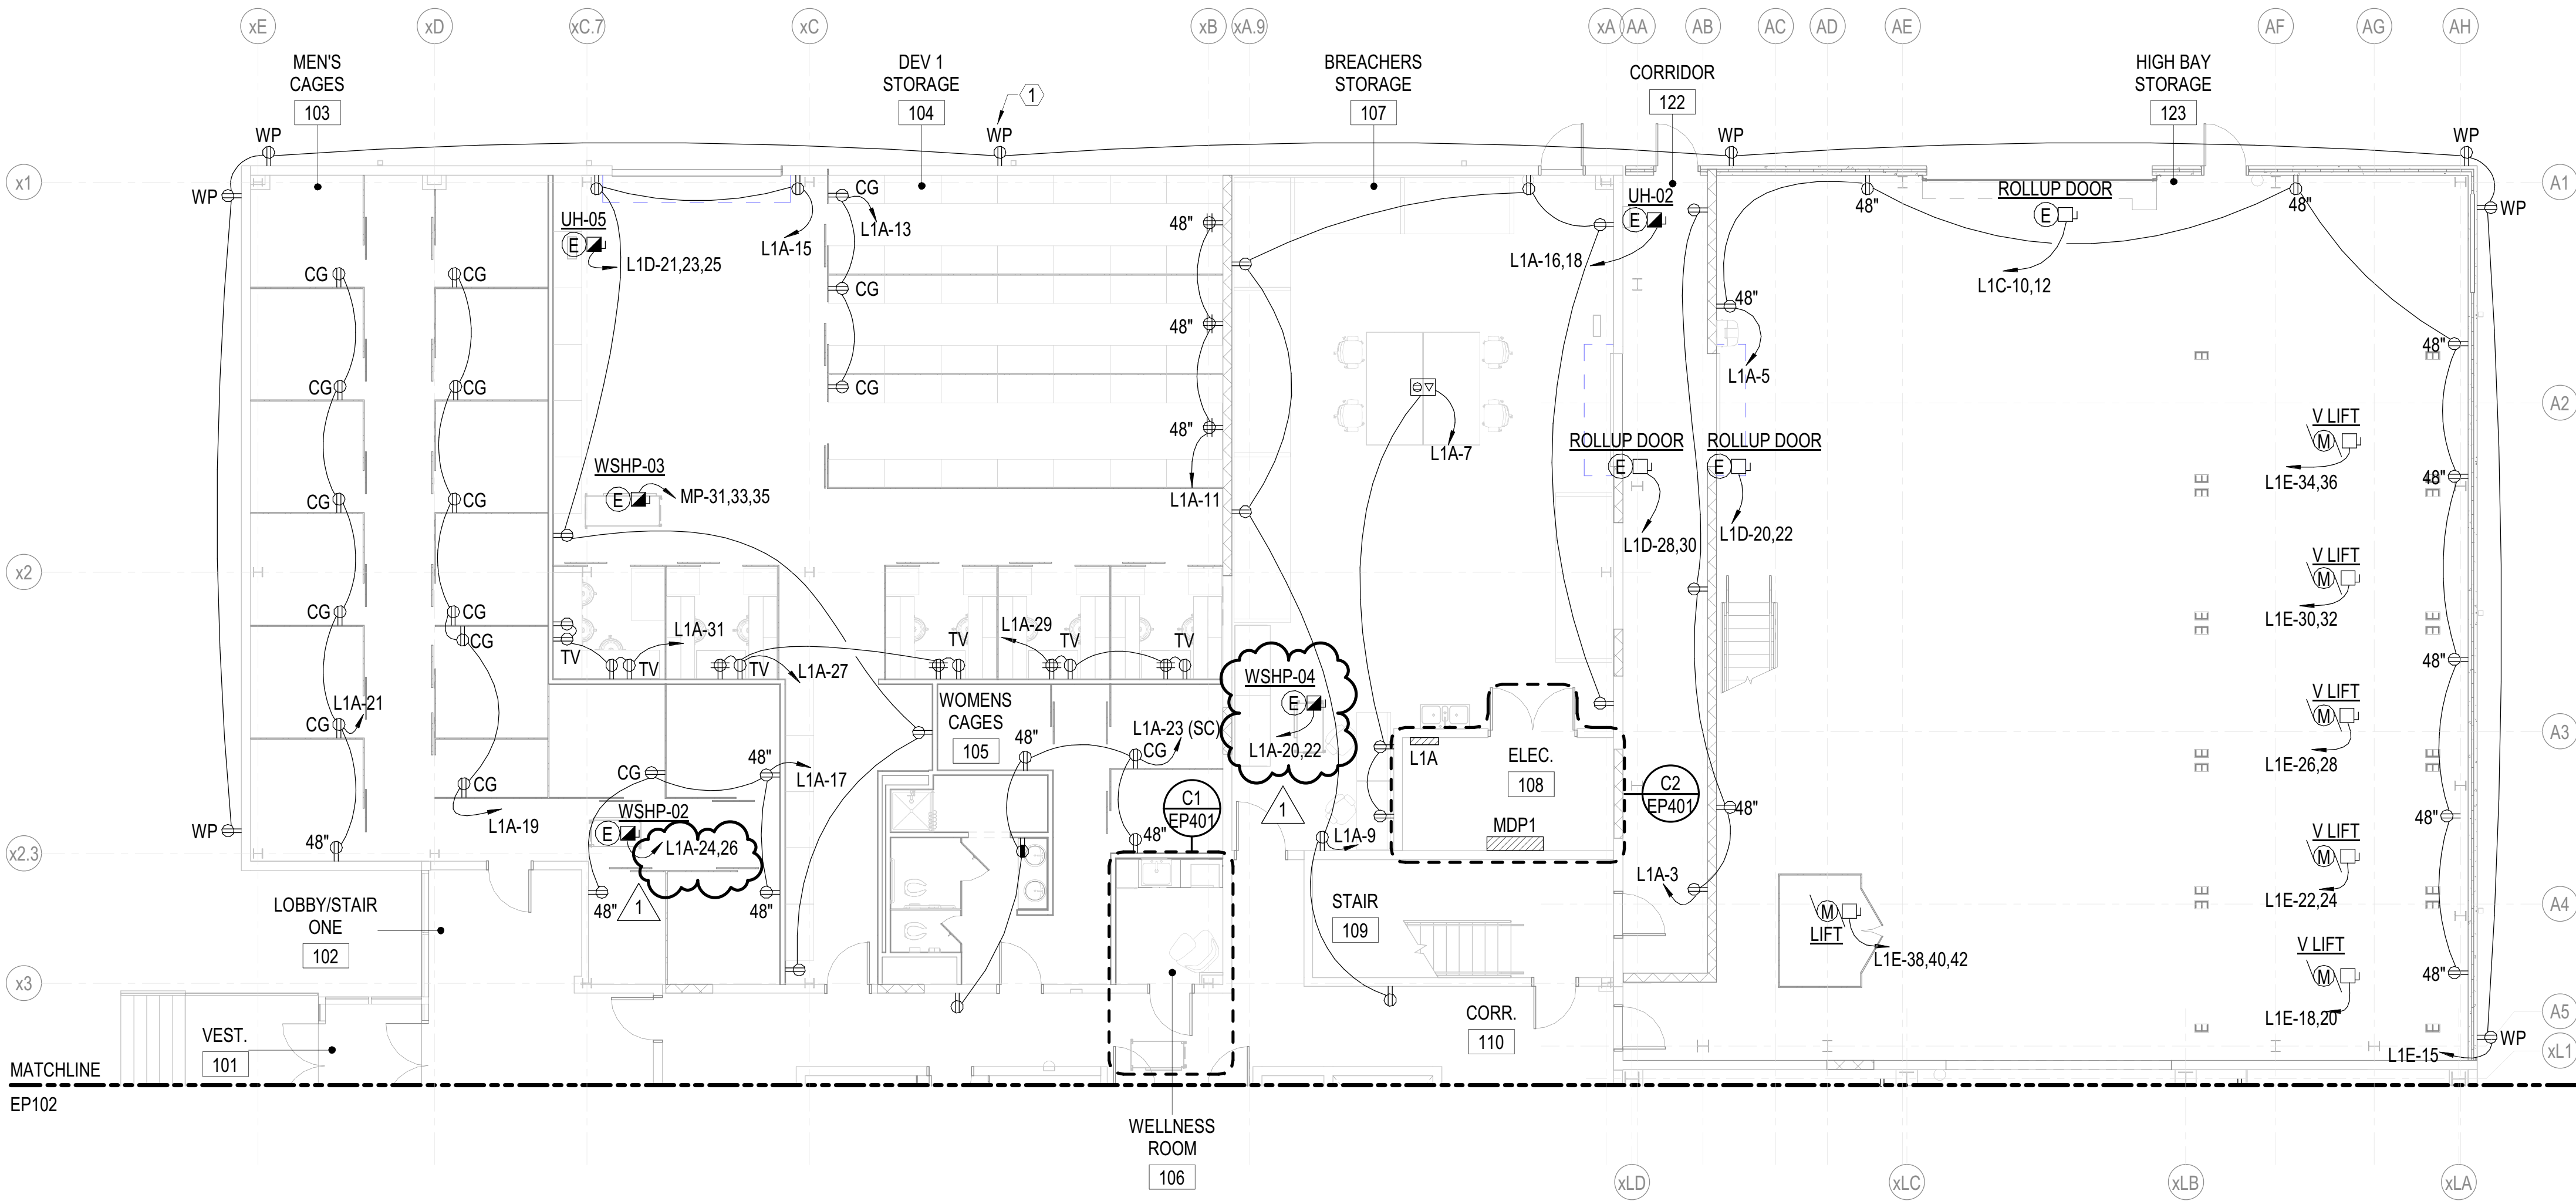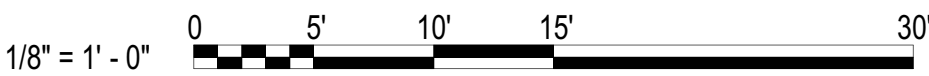

FIRST FLOOR PLAN AREA A - POWER

NOT TO SCALE

1

2

3

UNCLASSIFIED

4

5

1

2

3

UNCLASSIFIED

4

5

GENERAL SHEET NOTES

SHEET KEYNOTES

- 1 REUSE JUNCTION BOX ABANDONED DURING DEMOLITION OF EXISTING RECEPTACLE. PROVIDE EXTENSION RING.
- 2 THE WALK-IN FREEZER MUST REMAIN OPERATIONAL WITH MINIMAL DISCONNECTION DURING CONSTRUCTION. PROVIDE A PORTABLE GENERATOR AS REQUIRED TO MAINTAIN SERVICE TO WALK-IN FREEZER.



CLARKNEXSEN
4525 MAIN STREET SUITE 1400
VIRGINIA BEACH, VA 23462
757-455-5800 FAX 757-455-5638
WWW.CLARKNEXSEN.COM

FOR COMMANDER NAVFAC

ACTIVITY Approved by Don Bryant, PE, N10
Facilities Engineer, NSWDG
via Email

SATISFACTORY TO DATE 07/09/2025

DES BSP DRW MSW CHK SPS

PMIDM JT/SW

BRANCH MANAGER WRB

CHIEF ENGINEER JWJ

FIRE PROTECTION HPN

NAVAL FACILITIES ENGINEERING SYSTEMS COMMAND

NAVAL FACILITIES ENGINEERING SYSTEMS COMMAND - MID-ATLANTIC

NAVAL STATION - NORFOLK, VA

NAS OCEANA, DAM NECK ANNEX

Q-1075 SOF OPERATIONS BUILDING ADDITION

FIRST FLOOR PLAN AREA B - POWER

SCALE: AS NOTED

PROJECT NO.: 1625040

CONSTR. CONTR. NO. N40085-19-D-9041


NAVFAC DRAWING NO. 12929088

SHEET 183 OF 239


EP102

DRAWING REVISION: 25 AUGUST 2020

KEY PLAN

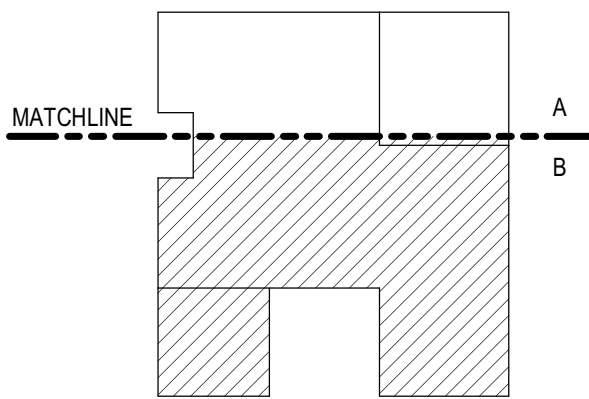

GRAPHIC SCALE(S)

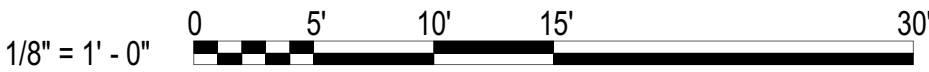

1

2

3

UNCLASSIFIED

4

5

D

C

B

A

D

C

B

A

1

2

3

UNCLASSIFIED

4

5

GENERAL SHEET NOTES

SHEET KEYNOTES

2 PROVIDE NEW STARTERS AND DISCONNECT SWITCHES TO REFEED ROOF MOUNTED EXHAUST FAN INDICATED.



CLARKNEXSEN
A JMT Company
4525 MAIN STREET SUITE 1400
VIRGINIA BEACH, VA 23462
757-455-5800 FAX 757-455-5638
WWW.CLARKNEXSEN.COM

APPROVED

FOR COMMANDER NAVFAC

ACTIVITY
Approved by Don Bryant, PE, N10
Facilities Engineer, NSWDG
via Email

SATISFACTORY TO DATE 07/09/2025

DES BSP | DRW MSW | CHK SPS

PMIDM JT/SW

BRANCH MANAGER WRB

CHIEF ENGINEER JWJ

FIRE PROTECTION HPN

NAVAL FACILITIES ENGINEERING SYSTEMS COMMAND

NAVAL FACILITIES ENGINEERING SYSTEMS COMMAND - MID-ATLANTIC

NAVAL STATION - NORFOLK, VA

NAS OCEANA, DAM NECK ANNEX

Q-1075 SOF OPERATIONS BUILDING ADDITION

VIRGINIA BEACH, VA

SECOND FLOOR PLAN AREA B - POWER

SCALE: AS NOTED

PROJECT NO.: 1625040

CONSTR. CONTR. NO. N40085-19-D-9041


NAVFAC DRAWING NO. 12929090

SHEET 185 OF 239


EP104

DRAWING REVISION: 25 AUGUST 2020

KEY PLAN

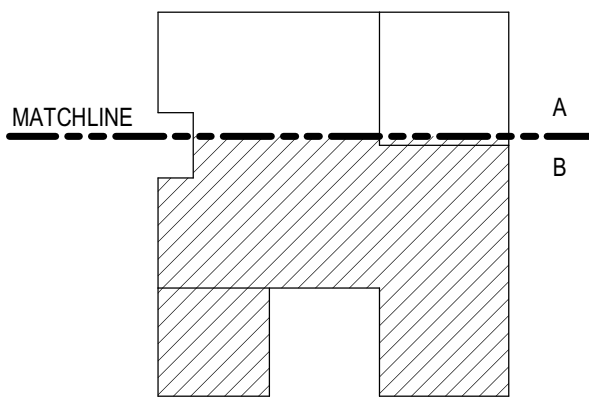

GRAPHIC SCALE(S)

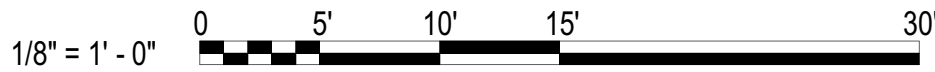

1

2

3

UNCLASSIFIED

4

5

D

C

B

A

D

C


UNCLASSIFIED

B

A

11/20/2025 8:38:32 AM
C:\Users\Brian.Pacansky\Documents\B\LOG\1075-1625040-E_Brian.Pacansky\QBK\EP105.rvt

EP105

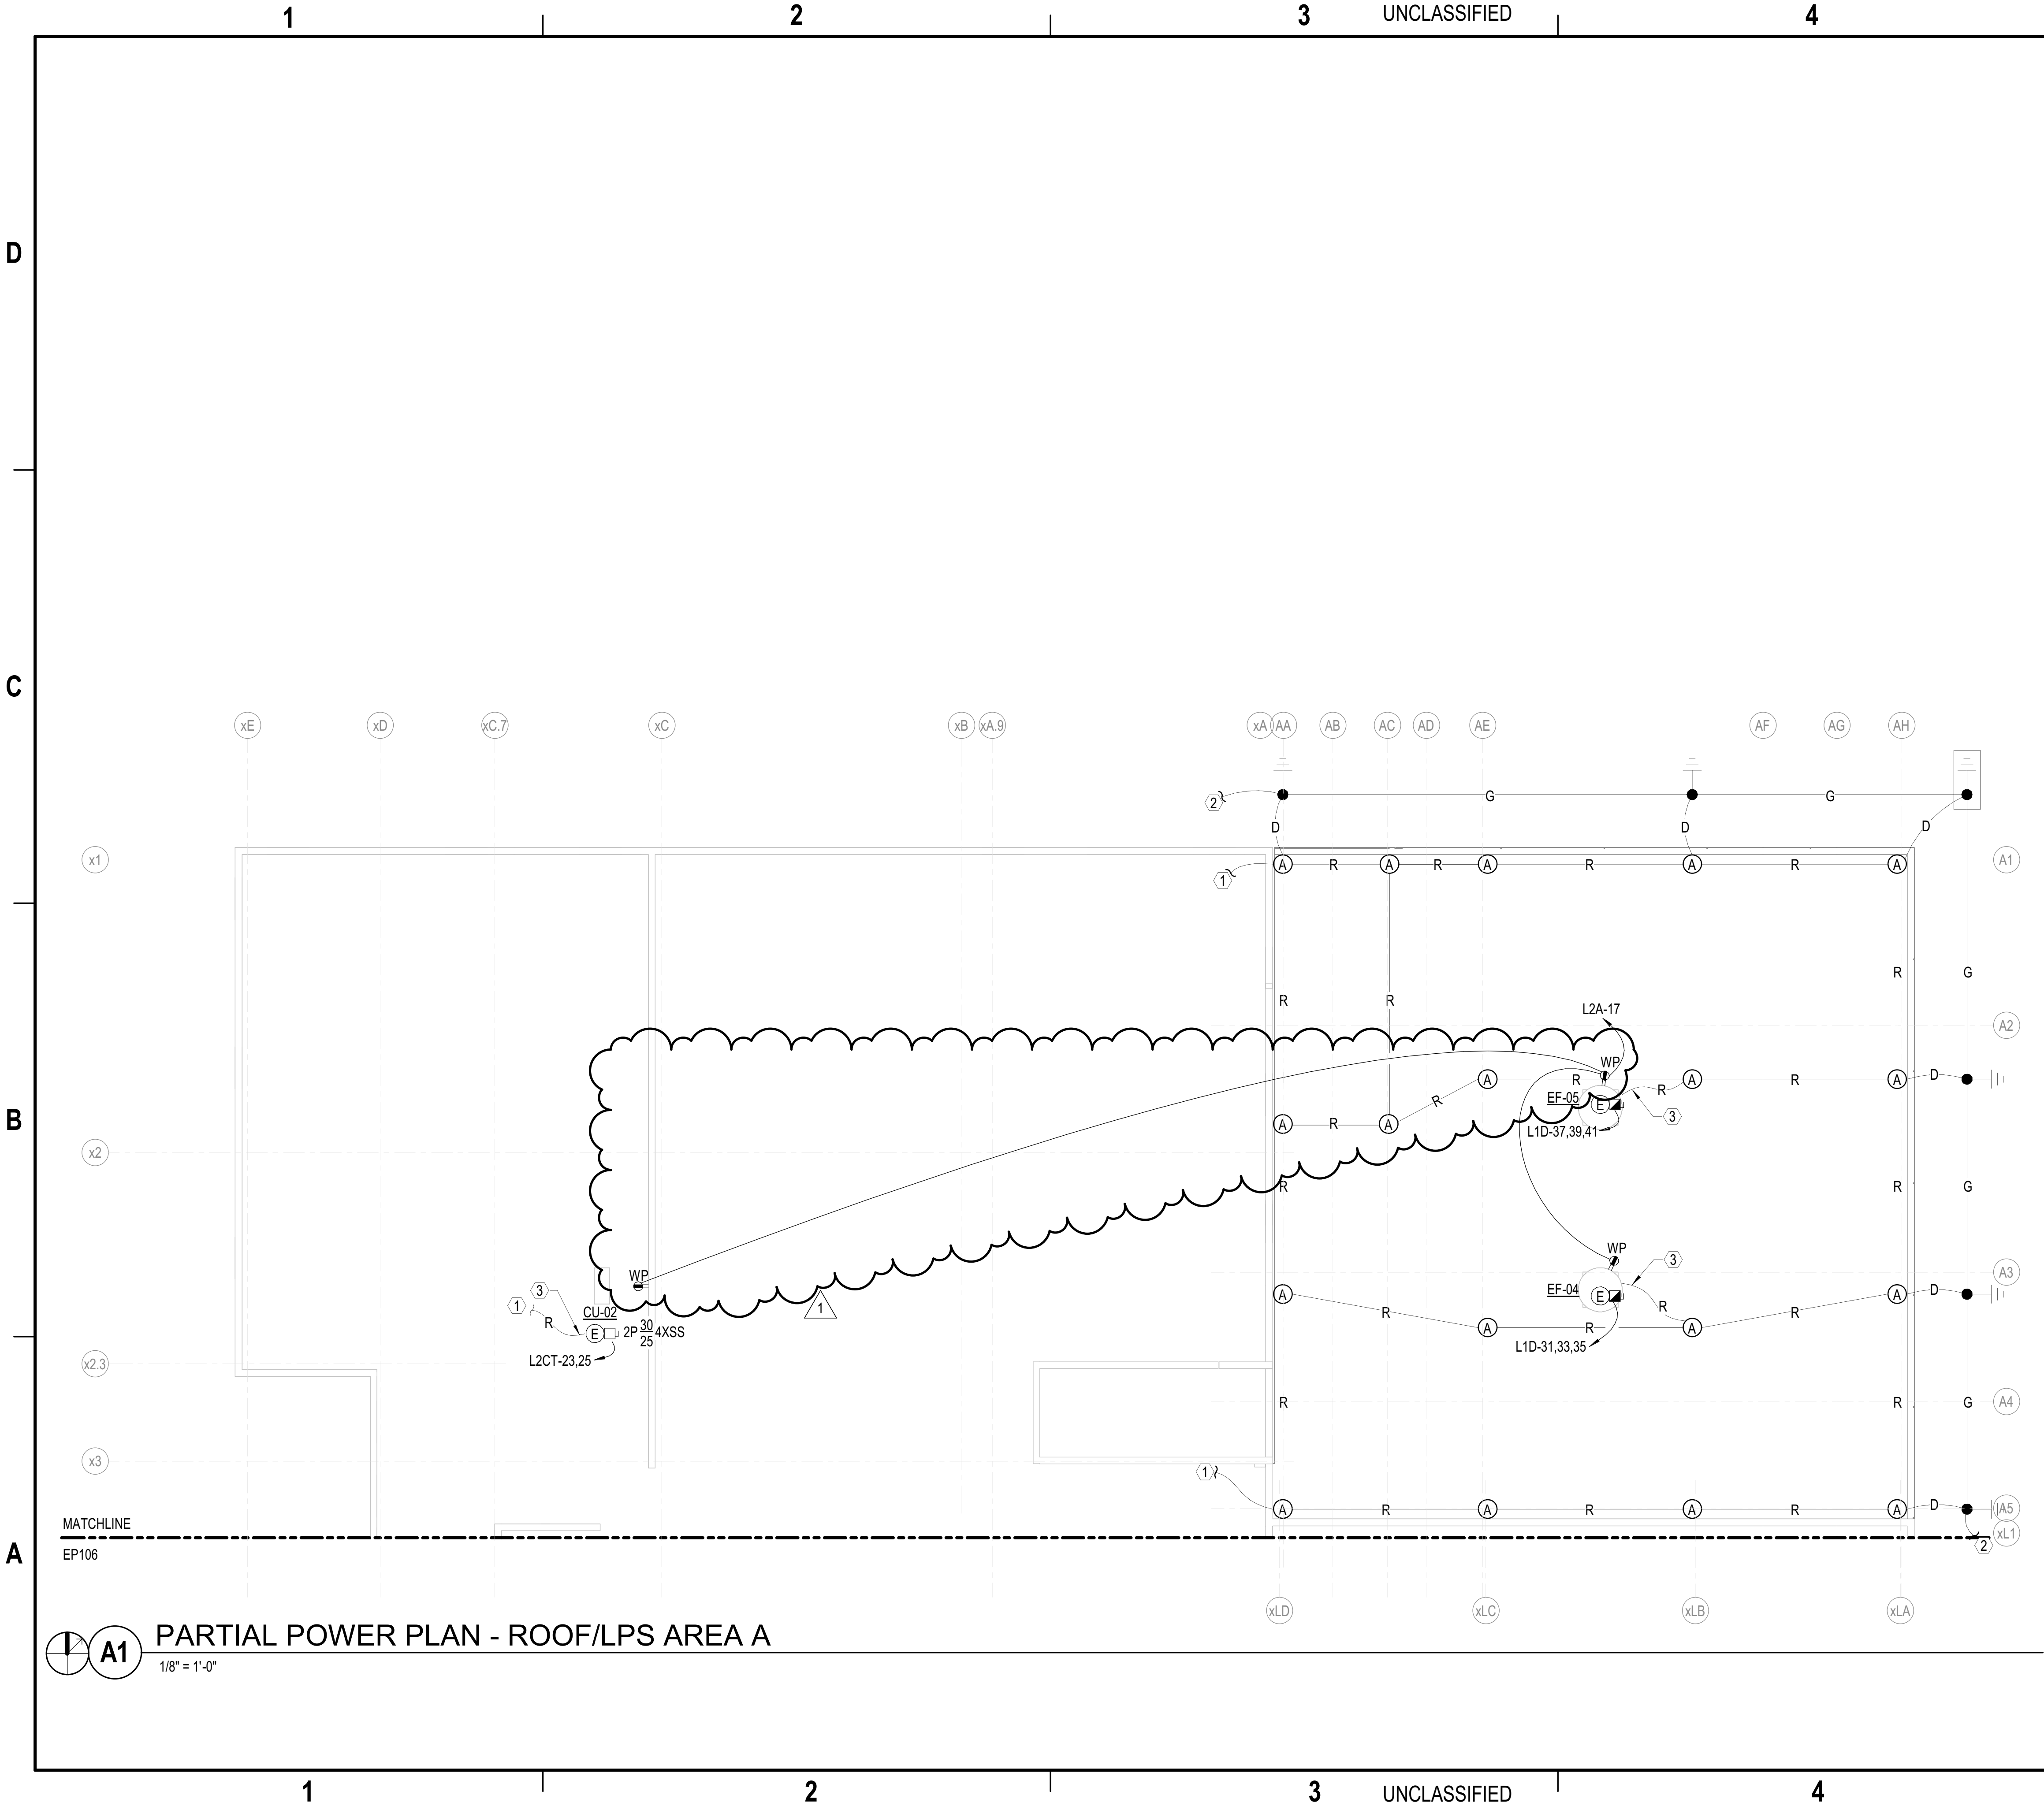

GENERAL SHEET NOTES

A. THE LIGHTNING PROTECTION SYSTEM LAYOUT AS SHOWN IS INTENDED TO DEPICT THE AREA OF COVERAGE AND GENERAL LAYOUT, BUT IS NOT REPRESENTATIVE OF ALL THE COMPONENTS REQUIRED. THE LIGHTNING PROTECTION SYSTEM INSTALLER MUST PROVIDE A COMPLETE SYSTEM IN ACCORDANCE WITH THE APPROVED SHOP DRAWING.

SHEET KEYNOTES

- 1 PROVIDE CONNECTION TO EXISTING LIGHTNING PROTECTION ROOF CONDUCTORS.
- 2 PROVIDE CONNECTION TO EXISTING GROUND LOOP CONDUCTORS.
- 3 PROVIDE CONNECTION TO EQUIPMENT INDICATED.



CLARK NEXSEN
A JMT Company
4525 MAIN STREET
SUITE 1400
VIRGINIA BEACH, VA 23462
757-455-5800 FAX 757-455-5638
WWW.CLARKNEXSEN.COM

APPROVED

FOR COMMANDER NAVAC

ACTIVITY
Approved by Don Bryant, PE, N10
Facilities Engineer, NSWDG
via Email

SATISFACTORY TO DATE 07/09/2025

DES BSP | DRW MSW | CHK SPS

PMIDM JT/SW

BRANCH MANAGER WRB

CHIEF ENGINEER JWJ

FIRE PROTECTION HPN

NAVAL FACILITIES ENGINEERING SYSTEMS COMMAND

NAVAL FACILITIES ENGINEERING SYSTEMS COMMAND - MID-ATLANTIC

NAVAL STATION - NORFOLK, VA

NAS OCEANA, DAM NECK ANNEX

Q-1075 SOF OPERATIONS BUILDING ADDITION

PARTIAL POWER PLAN - ROOF/LPS AREA A

SCALE: AS NOTED

PROJECT NO.: 1625040

CONSTR. CONTR. NO. N40085-19-D-9041


NAVAC DRAWING NO. 12929091

SHEET 186 OF 239

EP105

DRAWING REVISION: 25 AUGUST 2020

KEY PLAN

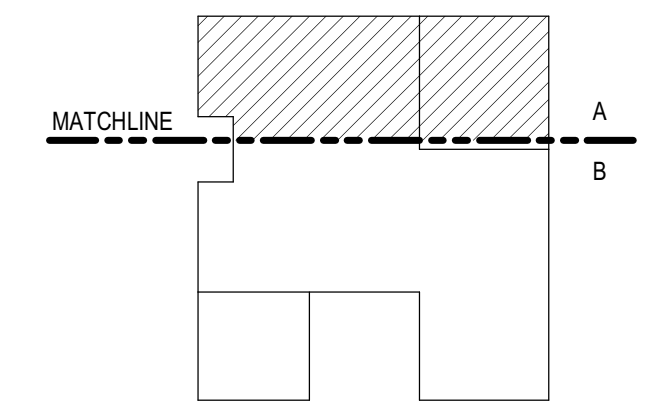

GRAPHIC SCALE(S)




D


C

B


A

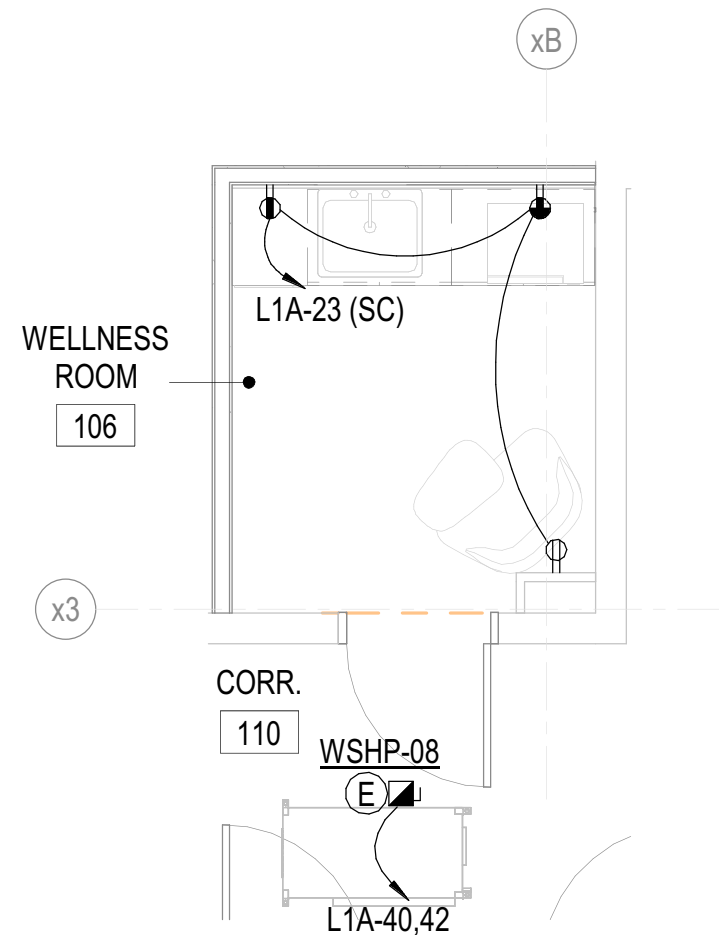


C1 ENLARGED POWER PLAN RM 106
1/4" = 1'-0"

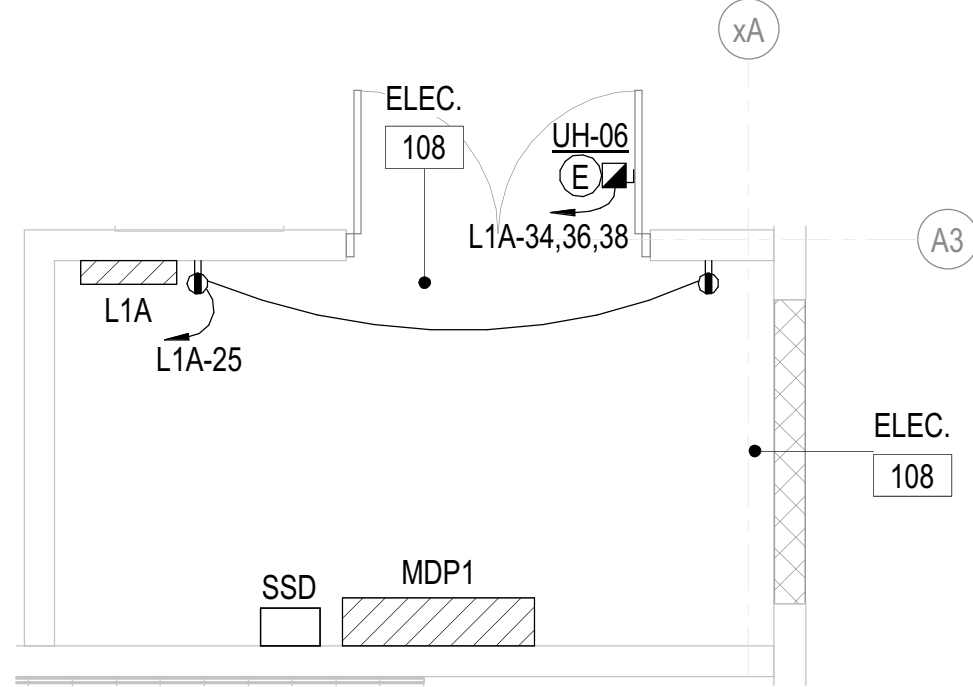


C2 ENLARGED POWER PLAN RM 108
1/4" = 1'-0"

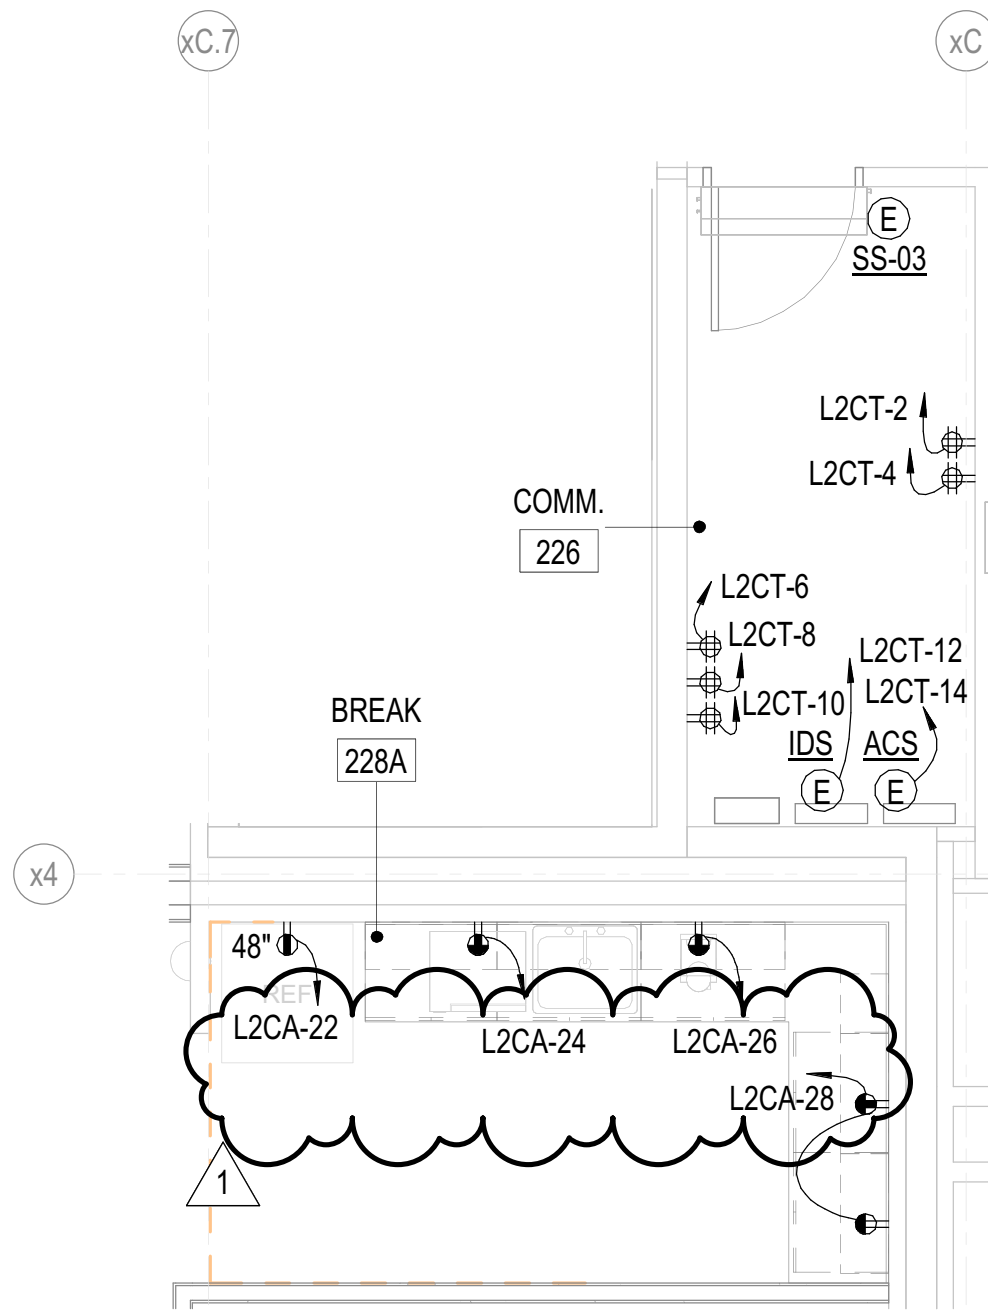


C3 ENLARGED POWER RMS 226 & 229
1/4" = 1'-0"

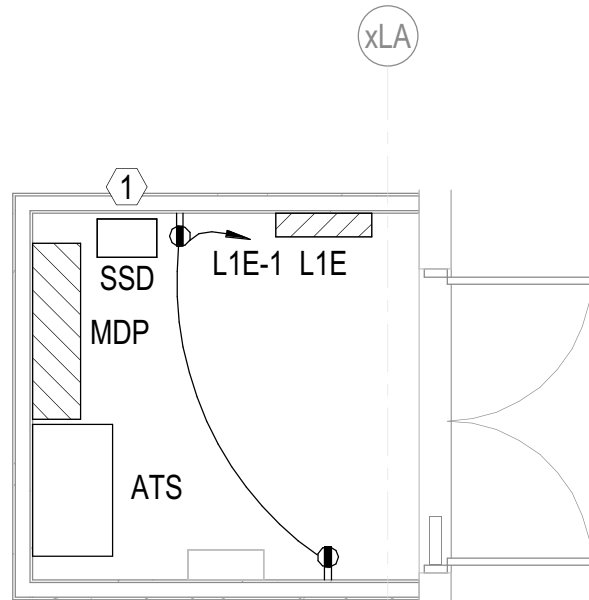


C5 ENLARGED POWER PLAN RM 125
1/4" = 1'-0"

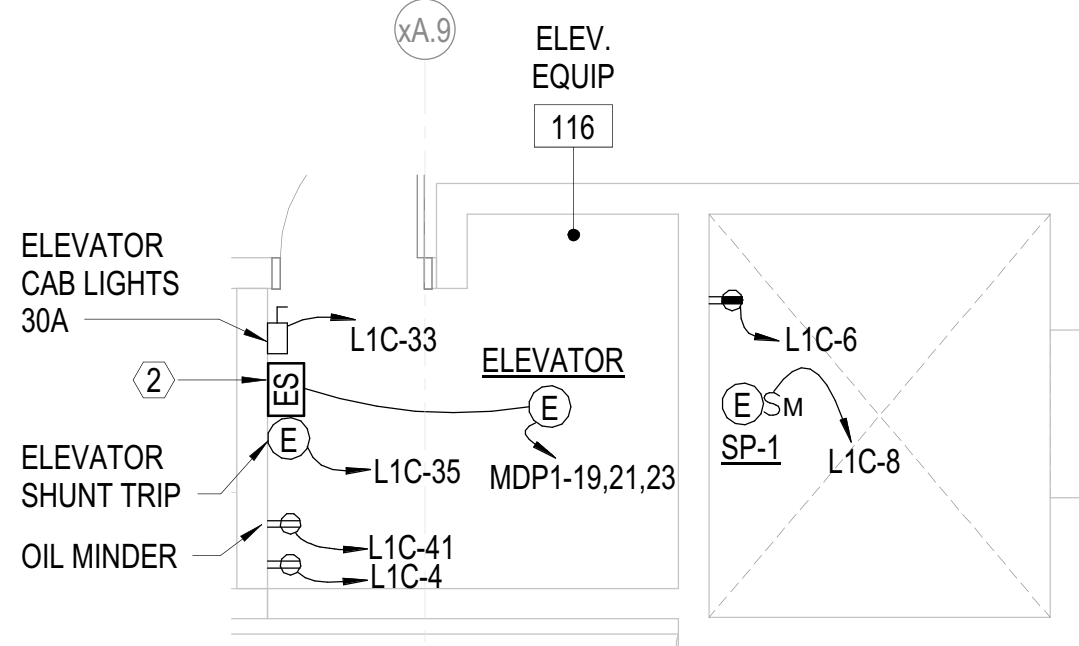

A1 ENLARGED POWER PLAN RM 116
1/4" = 1'-0"

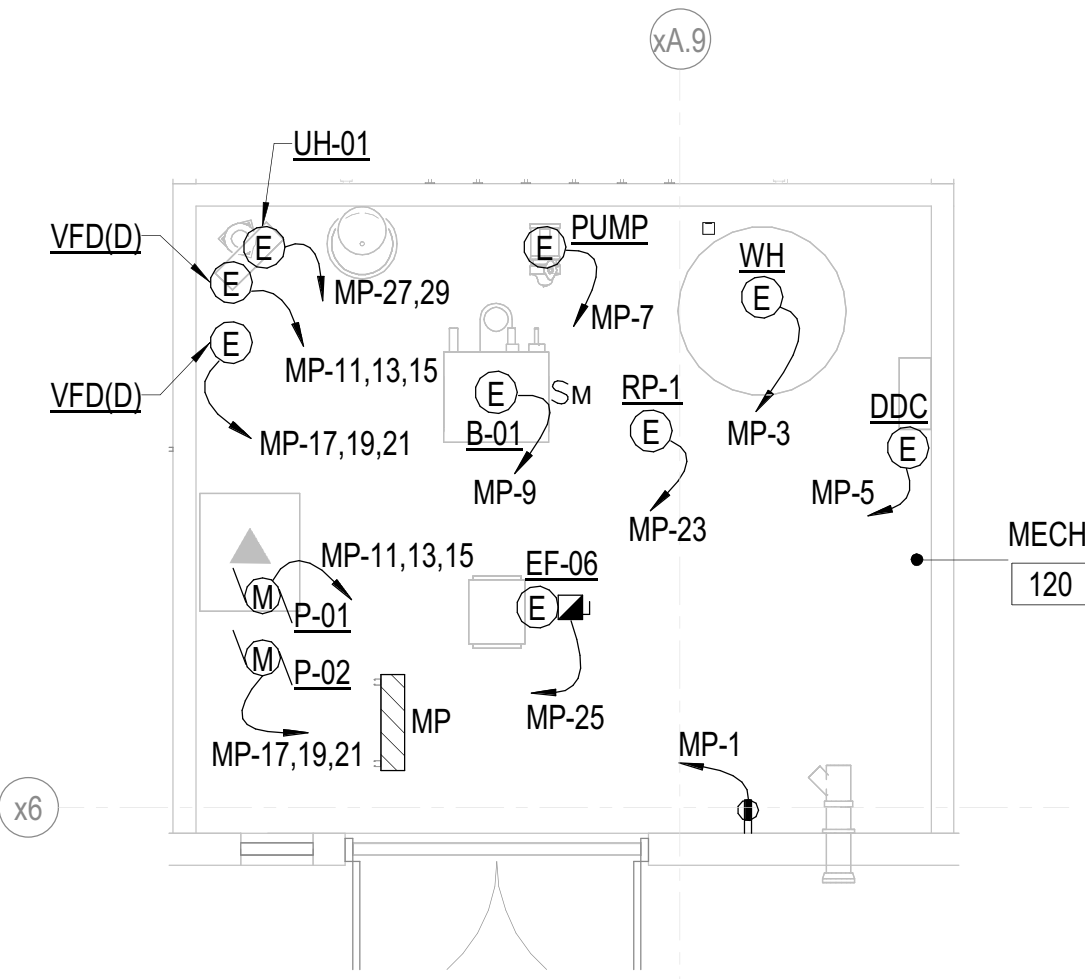


A2 ENLARGED POWER PLAN RM 120
1/4" = 1'-0"

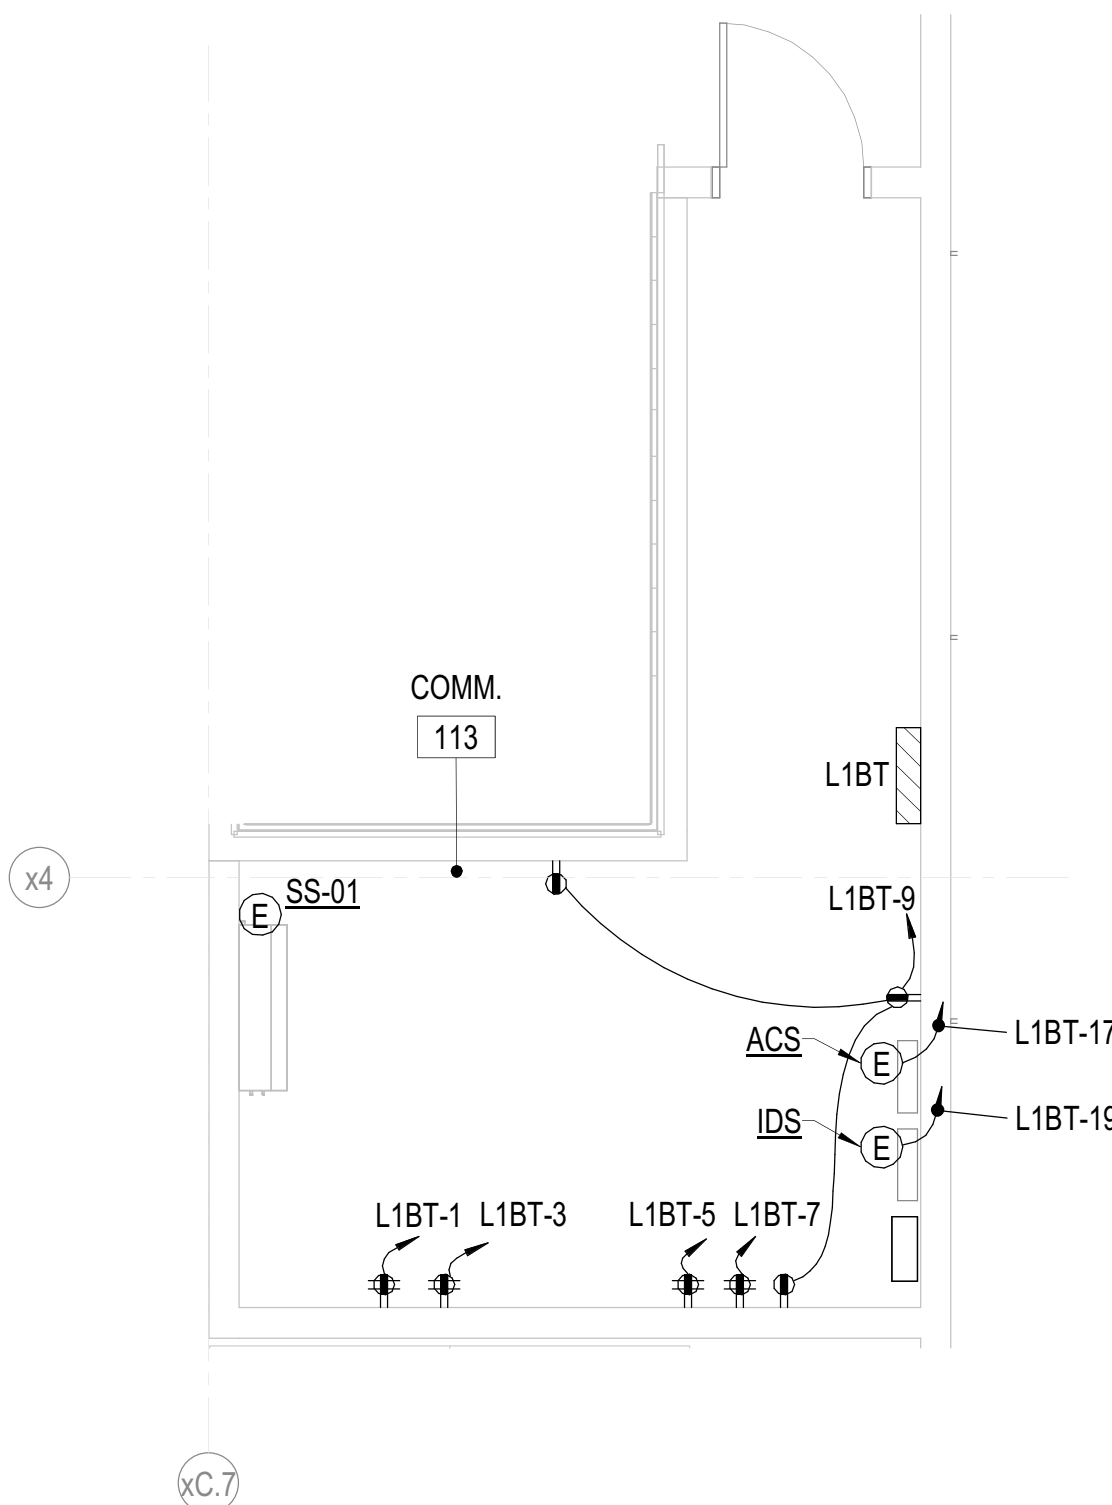

A3 ENLARGED POWER PLAN RM 113
1/4" = 1'-0"

SHEET KEYNOTES

- 1 LOCATE SURGE SUPPRESSION DEVICE SO THE BOTTOM IS AT 6'-6" AFF, ABOVE PANEL MDP WORKING CLEARANCE.
- 2 200A ELEVATOR CONTROL SWITCH WITH INTEGRAL SHUNT TRIP AND AUXILIARY STATUS RELAYS.

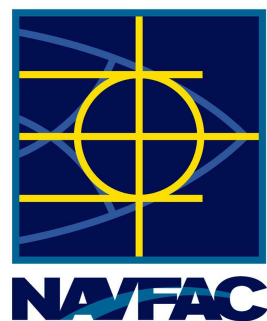

CLARK NEXSEN
A JMT Company
4525 MAIN STREET SUITE 1400
VIRGINIA BEACH, VA 23462
757-455-5800 FAX 757-455-5638
WWW.CLARKNEXSEN.COM

APPROVED
FOR COMMANDER NAVFAC
ACTIVITY
Approved by Don Bryant, PE, N10
Facilities Engineer, NSWDG
via Email
SATISFACTORY TO DATE 07/09/2025
DES BSP DRW MSW CHK SPS
PMDM JT/SW
BRANCH MANAGER WRB
CHIEF ENGINEER JWJ
FIRE PROTECTION HPN

DEPARTMENT OF THE NAVY
NAVAL FACILITIES ENGINEERING SYSTEMS COMMAND
NAVAL FACILITIES ENGINEERING SYSTEMS COMMAND - MID-ATLANTIC
NAVAL STATION - NORFOLK, VA
NAS OCEANA, DAM NECK ANNEX
Q-1075 SOF OPERATIONS BUILDING ADDITION
ENLARGED PLANS, MAIN ELEC ROOM, ELEC & CLOSETS

SCALE: AS NOTED
EPROJCT NO.: 1625040
CONSTR. CONTR. NO. N40085-19-D-9041
NAVFAC DRAWING NO. 12929093
SHEET 188 OF 239

EP401

DRAWING REVISION: 25 AUGUST 2020

PANEL L1A SCHEDULE

		225 AMP MLO		208Y/120 VOLTS		3PH, 4W, SN		MIN. 10 KAIC		SURFACE MOUNTED			
CKT. NO.	LOAD DESCRIPTION	COND SIZE	WIRE SIZE	BKR TRIP	AMPS	KVA	PH	KVA	AMPS	BKR TRIP	WIRE SIZE	COND SIZE	LOAD DESCRIPTION
1	REC EWC 107	3/4	12	20	4.0	0.5	A	1.6	13.0	20	12	3/4	LTS 102,110,107,122
3	REC CORR 122	3/4	12	20	6.0	0.7	B	1.3	10.9	20	12	3/4	LTS 104,105,106
5	REC HIGH BAY 123	3/4	12	20	12.0	1.4	A	1.4	11.9	20	12	3/4	LTS 103,104
7	REC BREACHERS 107	3/4	12	20	4.5	0.5	A	0.4	3.0	20	12	3/4	LTS HIGH BAY 123
9	REC BREACHERS 107	3/4	12	20	13.5	1.6	B	0.4	3.3	20	12	3/4	LTS EXTERIOR EAST
11	REC DEV 104	3/4	12	20	9.0	1.1	A	1.2	11.9	15	12	3/4	LTS EXTERIOR WEST
13	REC DEV 104	3/4	12	20	10.5	1.3	A	0.4	3.0	20	12	3/4	LTS STAIR 3
15	REC DEV 104	3/4	12	20	7.5	0.9	B	1.5	14.4	20	12	3/4	UH-02
17	REC DEV 104	3/4	12	20	9.0	1.1	B	1.5	14.4	20	12	3/4	UH-02
19	REC MEN'S CAGES 103	3/4	12	20	9.0	1.1	A	1.2	11.9	15	12	3/4	WSHP-04
21	REC MEN'S CAGES 103	3/4	12	20	9.0	1.1	B	1.2	11.9	15	12	3/4	WSHP-02
23	REC WOMEN'S CAGE 105	3/4	12	20	12.0	1.4	A	0.9	8.2	15	12	3/4	WSHP-02
25	REC ELEC 108	3/4	12	20	3.0	0.4	A	0.9	8.2	15	12	3/4	WSHP-02
27	REC DEV 1 STOR SOUTH	3/4	12	20	9.0	1.1	B	0.9	8.2	15	12	3/4	WSHP-07
29	REC DEV 1 STOR SE	3/4	12	20	9.0	1.1	B	0.9	8.2	15	12	3/4	WSHP-07
31	REC DEV 1 STOR SW	3/4	12	20	6.0	0.7	A	0.9	8.2	15	12	3/4	UH-06
33	SYSTEM FURNITURE 104	3/4	12	20	0.9	0.1	B	1.7	13.8	20	12	3/4	UH-06
35	WSHP-06	3/4	8	40	22.4	2.7	A	1.7	13.8	20	12	3/4	WSHP-08
37	SPARE				22.4	2.7	A	0.7	7.0	15	12	3/4	WSHP-08
41	SPARE						A	0.7	7.0	15	12	3/4	WSHP-08
43	SPARE						A	0.7	7.0	15	12	3/4	WSHP-08
45	SPARE						B						BUSSED SPACE
47	SPARE						C						BUSSED SPACE
49	SPARE						A						BUSSED SPACE
51	SPARE						B						BUSSED SPACE
53	SPARE						C						BUSSED SPACE
TOTAL AMPS (CONN. LOAD)		A:			116.8		B:		125.3		C:		139.8
TOTAL AMPS (FEEDTHRU)		A:					B:		125.3		C:		139.8
TOTAL AMPS (CONN. LOAD + FEED-THRU)		A:			116.8		B:		125.3		C:		139.8
PANELBOARD OPTIONS:		PANELBOARD NOTES:											
		LOCATION: ELEC 124											

LOAD DESCRIPTION	PANEL CONN. LOAD	SUBFEED CONN. LOAD	FEEDTHRU CONN. LOAD	TOTAL LOAD	D.F. MULT.	TOTAL KVA DEMAND
LIGHTING	6.4	KVA	KVA	KVA	1.25	8.0
RECEPTACLES	13.9	KVA	KVA	KVA	1.25	17.4
MECH EQUIP	20.4	KVA	KVA	KVA	1.25	25.5
ELECTRIC HEAT	3.0	KVA	KVA	KVA	1.25	3.8
MISCELLANEOUS	2.2	KVA	KVA	KVA	1.00	2.2
ELEVATOR		KVA	KVA	KVA	0.80	
TOTALS (CONN. KVA)	45.8	KVA	KVA	KVA		46.2
TOTALS (CONN. KVA + 20%)	55.0	KVA	KVA	KVA		55.5
TOTALS (CONN. AMPS)	127.2	AMPS	AMPS	AMPS		128.3
TOTALS (CONN. AMPS + 20%)	152.7	AMPS	AMPS	AMPS		153.9

PANEL L1BT SCHEDULE

		225 AMP MLO		208Y/120 VOLTS		3PH, 4W, SN		MIN. 10 KAIC		SURFACE MOUNTED			
CKT. NO.	LOAD DESCRIPTION	COND SIZE	WIRE SIZE	BKR TRIP	AMPS	KVA	PH	KVA	AMPS	BKR TRIP	WIRE SIZE	COND SIZE	LOAD DESCRIPTION
1	REC 103 RACK	3/4	12	20	3.0	0.4	A			20			SPARE
3	REC 103 RACK	3/4	12	20	3.0	0.4	A			20			SPARE
5	REC 103 RACK	3/4	12	20	3.0	0.4	A			20			SPARE
7	REC 103 RACK	3/4	12	20	3.0	0.4	A			20			SPARE
9	REC 103 RACK	3/4	12	20	4.5	0.5	B			20			SPARE
11	CU-01SS	3/4	10	30	16.0	1.7	A			20			SPARE
13					16.0	1.7	A			20			SPARE
15	FIRE ALARM (NOTE 1)	3/4	12	20	5.0	0.6	B			20			SPARE
17	ACS 113	3/4	12	20	5.0	0.6	C			20			SPARE
19	IDS 113	3/4	12	20	2.0	0.2	A			20			SPARE
21	SPARE						B			20			SPARE
23	SPARE						C			20			SPARE
25	SPARE						A			20			SPARE
27	SPARE						B			20			SPARE
29	SPARE						C			20			SPARE
TOTAL AMPS (CONN. LOAD)		A:			21.8		B:		12.5		C:		21.8
TOTAL AMPS (FEEDTHRU)		A:					B:		12.5		C:		21.8
TOTAL AMPS (CONN. LOAD + FEED-THRU)		A:			21.8		B:		12.5		C:		21.8
PANELBOARD OPTIONS:		PANELBOARD NOTES:											
		1. LOCATION: COMM 105											
		PROVIDE RED, LOCKABLE BREAKER.											

LOAD DESCRIPTION	PANEL CONN. LOAD	SUBFEED CONN. LOAD	FEEDTHRU CONN. LOAD	TOTAL LOAD	D.F. MULT.	TOTAL KVA DEMAND
LIGHTING	2.0	KVA	KVA	KVA	1.25	2.5
RECEPTACLES	3.3	KVA	KVA	KVA	1.25	4.1
MECH EQUIP	1.4	KVA	KVA	KVA	1.25	1.8
ELECTRIC HEAT		KVA	KVA	KVA	1.00	
MISCELLANEOUS		KVA	KVA	KVA	0.80	
ELEVATOR		KVA	KVA	KVA		
TOTALS (CONN. KVA)	6.7	KVA	KVA	KVA		6.7
TOTALS (CONN. KVA + 20%)	8.1	KVA	KVA	KVA		8.1
TOTALS (CONN. AMPS)	18.7	AMPS	AMPS	AMPS		18.7
TOTALS (CONN. AMPS + 20%)	22.5	AMPS	AMPS	AMPS		22.5

PANEL L1C SCHEDULE

		225 AMP MLO		208Y/120 VOLTS		3PH, 4W, SN		MIN. 10 KAIC		SURFACE MOUNTED			
CKT. NO.	LOAD DESCRIPTION	COND SIZE	WIRE SIZE	BKR TRIP	AMPS	KVA	PH	KVA	AMPS	BKR TRIP	WIRE SIZE	COND SIZE	LOAD DESCRIPTION
1	REC MAINT 121	3/4	12	20	6.0	0.7	A	1.0	8.0	20	12	3/4	FREEZER LIGHTS AND DOOR HEATER
3	SPARE						B	0.2	1.5	20	12	3/4	REC ELEV 116
5	SPARE						C	0.2	1.5	20	12	3/4	REC ELEV FIT
7	REC CAGES 121	3/4	12	20	2.0	0.2	A	2.4	20.0	30	10	3/4	SP-1
9	REC CAGES 121	3/4	12	20	8.0	1.0	B	2.0	19.6	35	8	3/4	ROLLUP DOOR
11	DRYER 121 RIGHT	3/4	10	30	23.0	2.4	A	2.4	19.6				SPARE
13	DRYER 121 LEFT	3/4	10	30	23.0	2.4	B						SPARE
15							C	1.2	10.0	15	12	3/4	AD-1
17	SPARE						A	3.0	25.3	50	6	1	AC-1
19	REC CAGES 114	3/4	12	20	6.0	0.7	B	3.0	25.3				SPARE
21	REC CAGES 114,115	3/4	12	20	9.0	1.1	A	3.0	25.3				SPARE
23	REC CAGES 114	3/4	12	20	12.0	1.4	A	0.7	6.4	15	12	3/4	WSHP-09
25	REC CAGES 114	3/4	12	20	4.0	0.5	B	0.7	6.4				SPARE
27	EWIC	3/4	12	20	7.5	0.9	C						SPARE
29	REC 110	3/4	12	20	9.0	1.1	A	3.9	32.2	60	4	1-1/4	BRIDGE CRANE
31	REC HIGH BAY 112	3/4	12	20	6.0	0.6	B	3.9	32.2				SPARE
33	ELEVATOR CAB LIGHTS	3/4	12	20	1.0	0.1	C	3.9	32.2				SPARE
35	ELEVATOR SHUNT TRIP												SPARE
37	FREEZER	1	6	50	25.0	2.6	A						SPARE
39					25.0	2.6	B						SPARE
41	REC 114 OIL MINDER	3/4	12	20	5.0	0.6	C						SPARE
TOTAL AMPS (CONN. LOAD)		A:			166.2		B:		146.2		C:		150.9
TOTAL AMPS (FEEDTHRU)		A:					B:		146.2		C:		150.9
TOTAL AMPS (CONN. LOAD + FEED-THRU)		A:			166.2		B:		146.2		C:		150.9
PANELBOARD OPTIONS:		PANELBOARD NOTES:											
		LOCATION: CAGES 111											

LOAD DESCRIPTION	PANEL CONN. LOAD	SUBFEED CONN. LOAD	FEEDTHRU CONN. LOAD	TOTAL LOAD	D.F. MULT.	TOTAL KVA DEMAND
LIGHTING	8.5	KVA	KVA	KVA	1.25	10.6
RECEPTACLES	12.7	KVA	KVA	KVA	1.25	15.9
MECH EQUIP	3.0	KVA	KVA	KVA	1.25	3.8
ELECTRIC HEAT		KVA	KVA	KVA	1.00	
MISCELLANEOUS		KVA	KVA	KVA	0.80	
ELEVATOR		KVA	KVA	KVA		
TOTALS (CONN. KVA)	54.3	KVA	KVA	KVA		54.3
TOTALS (CONN. KVA + 20%)	65.1	KVA	KVA	KVA		65.1
TOTALS (CONN. AMPS)	150.6	AMPS	AMPS	AMPS		150.6
TOTALS (CONN. AMPS + 20%)	180.7	AMPS	AMPS	AMPS		180.7

PANEL L1D SCHEDULE

		225 AMP MLO				208Y/120 VOLTS				3PH, 4W, SN		MIN. 10 KAIC		SURFACE MOUNTED			
CKT. NO.	LOAD DESCRIPTION	COND SIZE	WIRE SIZE	BKR TRIP	AMPS	KVA	PH	KVA	AMPS	BKR TRIP	WIRE SIZE	COND SIZE	LOAD DESCRIPTION	CKT. NO.			
1	REC 111	3/4	12	20	7.5	0.9	A	0.9	7.5	20	12	3/4	REC CAGES 121	2			
3	REC HIGH BAY 112	3/4	12	20	6.0	0.7	B	1.1	9.0	20	12	3/4	REC 117, 121	2			
5	LTS STORAGE 111,113	3/4	12	20	6.2	0.7	A			20			SPARE	6			
7	LTS 117,118,119	3/4	12	20	5.3	0.6	A			20			SPARE	8			
9	LTS 116,115,114	3/4	12	20	10.6	1.3	B			20			SPARE	8			
11	LTS CAGES 121	3/4	12	20	6.0	0.7	A			20			SPARE	10			
13	LTS LOW C/BAY 121	3/4	12	20	6.7	0.9	A			20			SPARE	12			
15	WSHP-05	3/4	12	15	7.0	0.7	B			20			SPARE	14			
17					7.0	0.7	C			20			SPARE	16			
19	REC OUTSIDE SW	3/4	12	20	7.5	0.9	A	2.0	19.6	35	8	3/4	ROLLUP DOOR	18			
21	UH-05	3/4	12	50	11.5	2.5	B	2.0	19.6	20			SPARE	20			
23					21.0	2.5	C			20			SPARE	22			
25					14.4	1.5	A	2.0	19.6	35	8	3/4	ROLLUP DOOR	24			
27	UH-04	3/4	12	20	14.4	1.5	B	2.0	19.6	20			SPARE	26			
29					3.0	0.4	C	2.0	19.6	20			SPARE	28			
31	EF-04	3/4	12	15	3.0	0.4	A	0.6	7.2	20	12	3/4	HEAT TRAKE	30			
33					3.0	0.4	B			20			SPARE	32			
35					3.0	0.4	C			20			SPARE	34			
37	EF-05	3/4	12	15	3.0	0.4	A			20			SPARE	36			
39					3.0	0.4	B			20			SPARE	38			
41					3.0	0.4	C			20			SPARE	40			
TOTAL AMPS (CONN. LOAD)						A: 85.5	B: 111.4	C: 74.8							42		
TOTAL AMPS (FEEDTHRU)						A: 85.5	B: 111.4	C: 74.8									
TOTAL AMPS (CONN. LOAD + FEED-THRU)																	
PANELBOARD OPTIONS:																	
LOCATION: CAGES 111																	

PANEL L2A SCHEDULE

225 AMP MLO															208Y/120 VOLTS															3PH, 4W, 3N															MIN. 10 KAIC															SURFACE MOUNTED														
CKT. NO.	LOAD DESCRIPTION	COND. SIZE	WIRE SIZE	BKR TRIP	AMPS	KVA	PH	KVA	AMPS	BKR TRIP	WIRE SIZE	COND. SIZE	LOAD DESCRIPTION	CKT. NO.	COND. SIZE	WIRE SIZE	BKR TRIP	AMPS	KVA	PH	KVA	AMPS	BKR TRIP	WIRE SIZE	COND. SIZE	LOAD DESCRIPTION	CKT. NO.	
1	2ND FLOOR LTS 235	3/4	12	20	10.9	1.3	A	0.7	6.0	20	12	3/4	SYSTEM FURNITURE 222	2	3/4	12	20	10.9	1.3	A	0.7	6.0	20	12	3/4	SYSTEM FURNITURE 222	4	
3	2ND FLOOR LTS 216,217,218-220	3/4	12	20	8.5	1.0	B	0.7	6.0	20	12	3/4	SYSTEM FURNITURE 222	6	3/4	12	20	8.5	1.0	B	0.7	6.0	20	12	3/4	SYSTEM FURNITURE 222	8	
5	SPARE							0.7	6.0	20	12	3/4	SYSTEM FURNITURE 222	10	3/4	12	20	8.1	1.0	B	0.7	7.0	15	12	3/4	WSHP-13	12	
7	2ND FLOOR LTS 228-229	3/4	12	20	6.0	0.7	A	0.7	6.0	20	12	3/4	SYSTEM FURNITURE 222	14	3/4	12	20	6.0	0.7	A	0.7	7.0	15	12	3/4	WSHP-09	16	
9	2ND FLOOR LTS HIGH BAY 112	3/4	12	20	8.1	1.0	B	0.7	7.0	15	12	3/4	WSHP-13	18	3/4	12	20	8.1	1.1	A	0.7	7.0	15	12	3/4	WSHP-20	20	
11	2ND FLOOR LTS 221-224,231-233	3/4	12	20	6.0	0.7	A	0.7	7.0	15	12	3/4	WSHP-09	22	3/4	12	20	4.5	0.5	A	2.0	16.6	30	10	3/4	WSHP-20	24	
13	SPARE							0.7	7.0	15	12	3/4	WSHP-09	26	3/4	12	20	9.1	1.1	A	0.7	7.0	15	12	3/4	WSHP-20	28	
15	2ND FLOOR 214	3/4	12	20	9.1	1.1	A	0.7	7.0	15	12	3/4	WSHP-20	30	3/4	12	20	4.5	0.5	A	2.0	16.6	30	10	3/4	WSHP-20	32	
17	REC ROOF	3/4	12	20	4.5	0.5	A	2.0	16.6	30	10	3/4	WSHP-20	34	3/4	12	20	16.6	1.8	B	2.0	16.6	30	10	3/4	WSHP-21	36	
19	SPARE							2.0	16.6	30	10	3/4	WSHP-20	38	3/4	12	20	16.6	1.8	B	2.0	16.6	30	10	3/4	WSHP-21	40	
21	REC FIDGE 208 LEFT	3/4	12	20	1.5	0.2	A	2.0	16.6	30	10	3/4	WSHP-21	42	3/4	12	20	1.5	0.2	A	2.0	16.6	30	10	3/4	WSHP-21	44	
23	REC FIDGE 208 RIGHT	3/4	12	20	1.5	0.2	A	2.0	16.6	30	10	3/4	WSHP-21	46	3/4	12	20	1.5	0.2	A	2.0	16.6	30	10	3/4	WSHP-21	48	
25	SPARE							2.0	16.6	30	10	3/4	WSHP-21	50	3/4	12	20	1.5	0.5	A	1.6	12.9	20	12	3/4	WSHP-16	52	
27	SPARE							2.0	16.6	30	10	3/4	WSHP-21	54	3/4	12	20	5.0	0.5	A	1.6	12.9	20	12	3/4	WSHP-16	56	
29	WSHP-22	3/4	12	15	5.0	0.5	A	1.6	12.9	20	12	3/4	WSHP-16	58	3/4	12	20	5.0	0.5	A	1.6	12.9	20	12	3/4	WSHP-16	60	
31	SPARE							1.6	12.9	20	12	3/4	WSHP-16	62	3/4	12	20	5.0	0.5	A	1.6	12.9	20	12	3/4	WSHP-16	64	
33	SPARE							1.6	12.9	20	12	3/4	WSHP-16	66	3/4	12	20	5.0	0.5	A	1.6	12.9	20	12	3/4	WSHP-16	68	
35	SPARE							1.6	12.9	20	12	3/4	WSHP-16	70	3/4	12	20	5.0	0.5	A	1.6	12.9	20	12	3/4	WSHP-16	72	
37	SPARE							1.6	12.9	20	12	3/4	WSHP-16	74	3/4	12	20	5.0	0.5	A	1.6	12.9	20	12	3/4	WSHP-16	76	
39	REC FIDGE 208 RIGHT	3/4	12	20	1.5	0.2	A	1.2	11.9	15	12	3/4	WSHP-14	78	3/4	12	20	1.5	0.2	A	1.2	11.9	15	12	3/4	WSHP-14	80	
41	REC COUNTER 208 LEFT	3/4	12	20	1.5	0.2	A	1.2	11.9	15	12	3/4	WSHP-14	82	3/4	12	20	1.5	0.2	A	1.2	11.9	15	12	3/4	WSHP-14	84	
43	REC COUNTER 208 RIGHT	3/4	12	20	1.5	0.2	A	0.9	7.5	20	12	3/4	REC 206 WSW	86	3/4	12	20	1.5	0.2	A	0.9	7.5	20	12	3/4	REC 206 WSW	88	
45	REC COUNTER 208 LEFT	3/4	12	20	1.5	0.2	A	0.9	7.5	20	12	3/4	REC 206 WSW	90	3/4	12	20	1.5	0.2	A	0.9	7.5	20	12	3/4	REC 206 WSW	92	
47	SPARE							0.4	4	25	12	3/4	REC 206 NW	94	3/4	12	20	1.5	0.4	A	0.4	4	25	12	3/4	REC 206 NW	96	
49	REC 206 SE	3/4	12	20	10.5	1.3	A	0.7	7.0	15	12	3/4	WSHP-23	98	3/4	12	20	10.5	1.3	A	0.7	7.0	15	12	3/4	WSHP-23	100	
51	REC 206 PERIM	3/4	12	20	7.5	0.9	A	0.7	7.0	15	12	3/4	WSHP-23	102	3/4	12	20	7.5	0.9	A	0.7	7.0	15	12	3/4	WSHP-23	104	
53	REC 206 SW	3/4	12	20	10.0	0.7	A	0.7	7.0	15	12	3/4	WSHP-23	106	3/4	12	20	10.0	0.7	A	0.7	7.0	15	12	3/4	WSHP-23	108	
TOTAL AMPS (CONN. LOAD)		A:		131.7		B:		117.4		C:		114.8		D:		114.8		E:		117.4		F:		114.8		G:	
TOTAL AMPS (FEEDTHRU)		A:		131.7		B:		117.4		C:		114.8		D:		114.8		E:		117.4		F:		114.8		G:	
TOTAL AMPS (CONN. LOAD + FEED-THRU)		A:		131.7		B:		117.4		C:		114.8		D:		114.8		E:		117.4		F:		114.8		G:	

TOTAL AMPS (CONN. LOAD)	A: 131.7	B: 117.4	C: 114.8
TOTAL AMPS (FEED-THRU)	A: 131.7	B: 117.4	C: 114.8
TOTAL AMPS (CONN. LOAD + FEED-THRU)	A: 131.7	B: 117.4	C: 114.8

LOAD DESCRIPTION	PANEL CONN. LOAD	SUBFEED CONN. LOAD	FEEDTHRU CONN. LOAD	TOTAL LOAD	D.F. MULT.	TOTAL KVA DEMAND
LIGHTING	5.8 KVA	KVA	KVA	5.8 KVA	1.25	7.25 KVA
RECEPTACLES	10.9 KVA	KVA	KVA	10.9 KVA	1.00	10.9 KVA
MECH EQUIP	27.0 KVA	KVA	KVA	27.0 KVA	1.00	27.0 KVA
ELECTRIC HEAT	KVA	KVA	KVA	KVA	1.25	KVA
MISCELLANEOUS	KVA	KVA	KVA	KVA	1.00	KVA
ELEVATOR	KVA	KVA	KVA	KVA	0.80	KVA

TOTALS (CONN. KVA)	43.7 KVA	KVA	KVA	43.7 KVA	44.7 KVA
TOTALS (CONN. KVA + 20%)	52.4 KVA	KVA	KVA	52.4 KVA	53.6 KVA
TOTALS (CONN. AMPS)	121.2 AMPS	AMPS	AMPS	121.2 AMPS	124.0 AMPS
TOTALS (CONN. AMPS + 20%)	145.4 AMPS	AMPS	AMPS	145.4 AMPS	148.8 AMPS

PANEL L2B SCHEDULE

225 AMP MLO						208Y/120 VOLTS		3PH, 4W, 3N		MIN. 10 KAIC		SURFACE MOUNTED			
CKT. NO.	LOAD DESCRIPTION	COND. SIZE	WIRE SIZE	BKR TRIP	AMPS	KVA	PH	KVA	AMPS	BKR TRIP	WIRE SIZE	COND. SIZE	LOAD DESCRIPTION	CKT. NO.	
1	WSHP-24						A	1.8	15.0	20	12	3/4	REC OFFICE 219,220	2	
3							B			20			SPARE	4	
5							C			20			SPARE	6	
7	REC 209, 210	3/4	12	20	12.0	1.4	A	0.9	7.5	20	12	3/4	REC OFFICE 228 CORRIDOR	8	
9	REC 218	3/4	12	20	12.0	1.4	B	1.3	10.5	20	12	3/4	REC OFFICE 221	10	
11	SYSTEM FURNITURE 218	3/4	12	20	7.5	0.9	A	1.1	9.0	20	12	3/4	REC OFFICE 222,223	12	
13	SYSTEM FURNITURE 218	3/4	12	20	7.5	0.9	A	1.1	9.0	20	12	3/4	REC CONFERENCE 224	14	
15							B	1.4	12.0	20	12	3/4	REC FL CONF. 224	16	
17							C	1.4	12.0	20	12	3/4	REC CONF. 224	18	
19	SYSTEM FURNITURE 218	3/4	12	20	12.0	1.4	A	1.1	9.0	20	12	3/4	REC CONF. 224	20	
21							B	1.1	9.0	20	12	3/4	REC OFFICE 218	22	
23							C	1.1	9.0	20	12	3/4	REC OFFICE 218	24	
25	SYSTEM FURNITURE 218	3/4	12	20	12.0	1.4	A	1.1	9.0	20	12	3/4	REC OFFICE 218	26	
27	WSHP-17	3/4	10	30	16.6	2.0	B	16.6	2.0	20	12	3/4	REC 215, 217	28	
29							C			20			SPARE	30	
31							A			20			SPARE	32	
33	SPARE						B			20			SPARE	34	
35	REC 218 FL CORR	3/4	12	20	7.5	0.9	A	0.7	6.0	20	12	3/4	REC 215, 217	36	
37	REC 211	3/4	12	20	7.5	0.9	A			20			SPARE	38	
39	REC 209-211	3/4	12	20	13.5	1.6	A	0.5	4.0	20	12	3/4	EWIC CORR 213	40	
41	REC 208 PERIM	3/4	12	20	4.5	0.5	A			20			SPARE	42	
43	SYSTEM FURNITURE 208	3/4	12	20	1.5	0.2	A			20			SPARE	44	
45	SYSTEM FURNITURE 208	3/4	12	20	1.5	0.2	A			20			SPARE	46	
47							B			20			SPARE	48	
49							C			20			SPARE	50	
51	REC 208 TABLE	3/4	12	20	6.0	0.7	A	2.0	16.6	30	10	3/4	WSHP-18	52	
53	REC 208 WEST	3/4	12	20	7.5	0.9	B	2.0	16.6					54	
TOTAL AMPS (CONN. LOAD)						A: 154.0	B:	132.5		C:	128.5				
TOTAL AMPS (FEEDTHRU)						A:	B:	132.5		C:	128.5				
TOTAL AMPS (CONN. LOAD + FEED-THRU)						A: 154.0	B: 132.5		C: 128.5					1	

TOTAL AMPS (CONN. LOAD)	A: 154.0	B: 132.5	C: 126.5
TOTAL AMPS (FEED-THRU)	A: 154.0	B: 132.5	C: 126.5
TOTAL AMPS (CONN. LOAD + FEED-THRU)	A: 154.0	B: 132.5	C: 126.5

LOAD DESCRIPTION	PANEL CONN. LOAD	SUBFEED CONN. LOAD	FEEDTHRU CONN. LOAD	TOTAL LOAD	D.F. MULT.	TOTAL KVA DEMAND
LIGHTING	32.0 KVA	KVA	KVA	32.0 KVA	1.25	40.0 KVA
RECEPTACLES	16.0 KVA	KVA	KVA	16.0 KVA	1.00	16.0 KVA
MECH EQUIP	1.8 KVA	KVA	KVA	1.8 KVA	1.00	1.8 KVA
ELECTRIC HEAT	KVA	KVA	KVA	KVA	1.25	KVA
MISCELLANEOUS	KVA	KVA	KVA	KVA	1.00	KVA
ELEVATOR	KVA	KVA	KVA	KVA	0.80	KVA

TOTALS (CONN. KVA)	49.8 KVA	KVA	KVA	49.8 KVA	38.8 KVA
TOTALS (CONN. KVA + 20%)	59.8 KVA	KVA	KVA	59.8 KVA	46.6 KVA
TOTALS (CONN. AMPS)	138.2 AMPS	AMPS	AMPS	138.2 AMPS	107.7 AMPS
TOTALS (CONN. AMPS + 20%)	165.8 AMPS	AMPS	AMPS	165.8 AMPS	129.3 AMPS

PANEL L2CA SCHEDULE

300 AMP MLO															FLUSH MOUNTED												
CKT. NO.	LOAD DESCRIPTION	COND. SIZE	WIRE SIZE	BKR TRIP	AMPS	KVA	PH	KVA	AMPS	BKR TRIP	WIRE SIZE	COND. SIZE	LOAD DESCRIPTION	CKT. NO.													
1	2ND FLOOR LTS 202,203	3/4	12	20	8.0	1.0	A	0.6	5.6	15	12	3/4	WSHP 19	2													
3	2ND FLOOR LTS 206-209	3/4	12	20	11.5	1.4	B	0.6	5.6	15	12	3/4	WSHP 19	4													
5	2ND FLOOR LTS 213,237	3/4	12	20	6.0	0.7	A	1.4	11.3	15	12	3/4	WSHP 10	6													
7	2ND FLOOR LTS HIGH BAY	3/4	12	20	11.0	1.3	A	1.4	11.3	15	12	3/4	WSHP 10	8													
9	SYSTEM FURNITURE 208	3/4	12	20	1.5	0.2	B	1.4	11.3	15	12	3/4	WSHP11	10													
11					1.5	0.2	A	1.4	11.3					12													
13					1.5	0.2	B	1.4	11.3					14													
15	SYSTEM FURNITURE 208	3/4	12	20	1.5	0.2	B	1.4	11.3					16													
17	2ND FLOOR 208 FL	3/4	12	20	7.5	0.9	A	0.5	4.0	15	12	3/4	WSHP 12	18													
19	WSHP 27	3/4	12	15	11.3	1.4	A	0.5	4.0	20	12	3/4	WSHP 12	20													
21					11.3	1.4	B	0.6	7.0	20	12	3/4	REC FRIDGE 228A	22													
23					11.3	1.4	A	0.2	1.5	20	12	3/4	REC 228A	24													
25	WSHP 28	3/4	12	15	5.0	0.5	A	0.2	1.5	20	12	3/4	REC 228A	26													
27					5.0	0.5	B	0.4	3.0	20	12	3/4	REC 228A	28													
29	WSHP 29	3/4	12	15	5.6	0.6	A	1.1	10.1	25	12	3/4	SPARE	30													
31					5.6	0.6	B	1.1	10.1	25	12	3/4	WSHP 25	32													
33	REC 206 SW 3	3/4	12	20	9.0	1.1	B	1.1	10.1					34													
35	SPARE						A			20			SPARE	36													
37	PANEL L2CT				50.1	6.0	A			20			SPARE	38													
39					29.4	3.5	B	0.9	7.5	20	12	3/4	REC 206 SW 2	40													
41					47.0	5.6	C			20			SPARE	42													
43	WSHP-26	3/4	12	20	12.9	1.6	A			20			SPARE	44													
45					12.9	1.6	B			20			SPARE	46													
47					12.9	1.6	C			20			SPARE	48													
49	PANEL L2CB				139.5	16.7	A			20			SPARE	50													
51					122.5	14.7	B			20			SPARE	52													
53					114.5	13.7	C			20			SPARE	54													
TOTAL AMPS (CONN. LOAD)					A:	285.6		B:	257.8	C:	234.1																
TOTAL AMPS (FEED-THRU)					A:	285.6		B:	257.8	C:	234.1																
TOTAL AMPS (CONN. LOAD + FEED-THRU)					A:	285.6		B:	257.8	C:	234.1																

D

C

B

A

D

C

UNCLASSIFIED

B

A

PANEL L1E SCHEDULE															
225 AMP MLO				208Y/120 VOLTS				3PH, 4W, SN		MIN. 10 KAIC		SURFACE MOUNTED			
CKT. NO.	LOAD DESCRIPTION	COND SIZE	WIRE SIZE	BKR TRIP	AMPS	KVA	PH	KVA	AMPS	BKR TRIP	WIRE SIZE	COND SIZE	LOAD DESCRIPTION	CKT. NO.	
1	REC ELEC 125	3/4	12	20	3.0	0.4	A			20			SPARE	2	
3	REC LOAD-OUT BAY 124	3/4	12	20	3.0	0.4	B			20			SPARE	4	
5	REC LOAD-OUT BAY 124	3/4	12	20	10.5	1.3				20			SPARE	6	
7	REC EXT EAST	3/4	12	20	3.0	0.4	A			20			SPARE	8	
9	EF-07	3/4	12	20	6.6	0.8	B	1.6	15.4	20	12	3/4	UH-07	10	
11	REC EXT SOUTH EAST	3/4	12	20	4.5	0.5	C	1.6	15.4				SPARE	12	
13	REC LOAD-OUT BAY 124	3/4	12	20	12.0	1.4	A			20			SPARE	14	
15	REC EXT NORTH	3/4	12	20	12.0	1.4	B	1.1	9.0	20	12	3/4	REC LOAD-OUT BAY 124	16	
17	ROLLUP DOOR	3/4	8	35	19.2	2.0	C	1.4	13.8	30	10	3/4	VEHICLE LIFT 5	18	
19					19.2	2.0	A	1.4	13.8					20	
21	ROLLUP DOOR	3/4	8	35	19.2	2.0	B	1.4	13.8	30	10	3/4	VEHICLE LIFT 4	22	
23					19.2	2.0	C	1.4	13.8					24	
25	EF-01	3/4	12	15	3.0	0.4	A	1.4	13.8	30	10	3/4	VEHICLE LIFT 3	26	
27					3.0	0.4	B	1.4	13.8					28	
29					3.0	0.4	C	1.4	13.8	30	10	3/4	VEHICLE LIFT 2	30	
31	EF-03	3/4	12	15	3.0	0.4	A	1.4	13.8	30	10	3/4	VEHICLE LIFT 1	32	
33					3.0	0.4	B	1.4	13.8					34	
35					3.0	0.4	C	1.4	13.8					36	
37	EF-02	3/4	12	15	3.0	0.4	A	3.9	32.2	60	4	1-1/4	MATERIAL LIFT	38	
39					3.0	0.4	B	3.9	32.2					40	
41					3.0	0.4	C	3.9	32.2					42	
43	BUSSED SPACE						A	0.6	5.0	20	12	3/4	CCC-CT	44	
45	BUSSED SPACE						B	0.7	7.0	15	12	3/4	CCC-HT (NOTE 1)	46	
47	BUSSED SPACE						A	0.7	7.0				BUSSED SPACE	50	
49	BUSSED SPACE						B						BUSSED SPACE	52	
51	BUSSED SPACE						C						BUSSED SPACE	54	
53	BUSSED SPACE												BUSSED SPACE		
TOTAL AMPS (CONN. LOAD)				A: 116.8				B: 143.8				C: 156.9			
TOTAL AMPS (FEEDTHRU)				A: 116.8				B: 143.8				C: 156.9			
TOTAL AMPS (CONN. LOAD + FEED-THRU)				A: 116.8				B: 143.8				C: 156.9			
PANELBOARD OPTIONS:				PANELBOARD NOTES:											
				LOCATION: ELEC 112											
				1. PROVIDE PROVISIONS TO LOCK BREAKER IN THE OPEN POSITION.											
				2. PROVIDE EQUIPMENT PROTECTION GROUND FAULT INTERRUPTER TYPE.											

A


B

C

D

PANEL MDP SCHEDULE																	
		2000 AMP MCB		208Y/120 VOLTS		3PH, 4W, SN		MIN. 25 KAIC		SURFACE MOUNTED		SE RATED					
CKT. NO.	LOAD DESCRIPTION	COND. SIZE	WIRE SIZE	BKR TRIP	AMPS	KVA	PH	KVA	AMPS	BKR TRIP	WIRE SIZE	COND. SIZE	LOAD DESCRIPTION	CKT. NO.			
1	BUSSED SPACE						A	14.0	116.8	225	*	*	PANEL L1E	2			
3							B	17.3	143.8					4			
5							C	18.8	156.9					6			
7	BUSSED SPACE						A			125			SPARE	8			
9							B							10			
11							C							12			
13	BUSSED SPACE						A	25.4	211.6	250	250	2-1/2	DOAS-01	14			
15							B	25.4	211.6					16			
17							C	25.4	211.6					18			
19	BUSSED SPACE						A	19.9	166.2	225	*	*	PANEL L1C	20			
21							B	17.5	146.2					22			
23							C	18.1	150.9					24			
25	PANEL MDP1	*	*		1103.9	132.5	A			60	4	1-1/4	SPD	26			
27					1058.5	127.0	B							28			
29					1016.8	122.0	C							30			
TOTAL AMPS (CONN. LOAD)					A:	1598.5	B:	1560.1	C:	1536.3							
TOTAL AMPS (FEEDTHRU)					A:		B:	1560.1	C:								
TOTAL AMPS (CONN. LOAD + FEED-THRU)					A:	1598.5	B:	1560.1	C:	1536.3							
PANELBOARD OPTIONS:					PANELBOARD NOTES:												
1. PROVIDE 100% RATED MCB.					LOCATION: ELEC 112												
2. PROVIDE EXTERNALLY MOUNTED SPD.					*** INDICATES SEE POWER RISER FOR FEEDER SIZING.												

LOAD DESCRIPTION	PANEL CONN. LOAD	SUBFEED CONN. LOAD	FEEDTHRU CONN. LOAD	TOTAL LOAD	D.F. MULT.	TOTAL KVA DEMAND
LIGHTING	KVA 20.8	KVA 20.8	KVA 20.8	KVA 20.8	KVA	1.25
RECEPTACLES	KVA 134.9	KVA 134.9	KVA 134.9	KVA 134.9	KVA	72.5
MECH EQUIP	KVA 189.6	KVA 189.6	KVA 189.6	KVA 189.6	KVA	1.00
ELECTRIC HEAT	KVA 26.2	KVA 26.2	KVA 26.2	KVA 26.2	KVA	1.25
MISCELLANEOUS	KVA 90.2	KVA 90.2	KVA 90.2	KVA 90.2	KVA	1.00
ELEVATOR	KVA 22.4	KVA 22.4	KVA 22.4	KVA 22.4	KVA	0.80
	KVA	KVA	KVA	KVA	KVA	
	KVA	KVA	KVA	KVA	KVA	
TOTALS (CONN. KVA)	76.2	KVA 484.1	KVA	KVA 560.3	KVA	505.1
TOTALS (CONN. KVA + 20%)	91.4	KVA 581.0	KVA	KVA 672.4	KVA	606.1
TOTALS (CONN. AMPS)	211.4	AMPS 1343.8	AMPS	AMPS 1555.2	AMPS	1402.1
TOTALS (CONN. AMPS + 20%)	253.7	AMPS 1612.6	AMPS	AMPS 1866.3	AMPS	1682.5

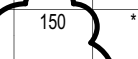PANEL MDP1 SCHEDULE																
						20BY120 VOLTS		3PH, 4W, 5N		MIN. 22 KAIC		SURFACE MOUNTED				
CKT. NO.	LOAD DESCRIPTION	CONN. SIZE	WIRE SIZE	BKR TRIP	AMPS	KVA	PH	KVA	AMPS	BKR TRIP	WIRE SIZE	COND. SIZE	LOAD DESCRIPTION	CKT. NO.		
1	SPARE			150			A						PANEL L1A	2		
3							B							4		
5							C	16.8	138.8					6		
7	PANEL L1BT	*	*	125	21.8	2.6	A	21.7	181.0	225	*	*	PANEL MP	8		
9					12.5	1.5	B	20.9	174.0					10		
11					21.8	2.6	A	21.1	175.5					12		
13	PANEL L1D	*	*	125	85.5	10.3	A	15.8	131.7		*	*	PANEL L2A	14		
15					111.4	13.4	B	14.1	117.6					16		
17					74.8	9.0	C	13.8	114.4					18		
19	ELEVATOR	1-1/2	1	125	62.1	7.5	A	18.5	154.0	150	*	*	PANEL L2B	20		
21					62.1	7.5	B	15.9	132.5					22		
23					62.1	7.5	C	15.4	128.5					24		
25	PANEL L2CA	*			285.6	34.3	A	7.9	65.5	125	1	1-1/2	CCC-1	26		
27					257.8	30.9	B	7.9	65.5					28		
29					234.1	28.1	C	7.9	65.5					30		
31	BUSSED SPACE						A						BUSSED SPACE	32		
33							B							34		
35							C							36		
37	SPD	1-1/4	4	60			A						BUSSED SPACE	38		
39							B							40		
41							C							42		
TOTAL AMPS (CONN. LOAD)					A: 1103.9		B: 1058.5		C: 1016.8							
TOTAL AMPS (FEEDTHRU)					A: 1103.9		B: 1058.5		C: 1016.8							
TOTAL AMPS (CONN. LOAD + FEEDTHRU)					A: 1103.9		B: 1058.5		C: 1016.8							
PANELBOARD OPTIONS:					PANELBOARD NOTES:											
1. PROVIDE EXTERNALLY MOUNTED SPD.					LOCATION: ELEC 124											
					1. *** INDICATES SEE POWER RISER FOR FEEDER SIZING.											

LOAD DESCRIPTION	PANEL CONN. LOAD	SUBFEED CONN. LOAD	FEEDTHRU CONN. LOAD	TOTAL LOAD	D.F. MULT.	TOTAL KVA DEMAND
LIGHTING	23.6	KVA 20.8	KVA	KVA 20.8	KVA 1.25	26.1
RECEPTACLES		KVA 118.8	KVA	KVA 118.8	KVA NEC	64.4
MECH EQUIP		KVA 148.0	KVA	KVA 171.6	KVA 1.00	171.6
ELECTRIC HEAT		KVA 23.0	KVA	KVA 23.0	KVA 1.25	28.7
MISC. LAUNDRUS		KVA 23.2	KVA	KVA 23.2	KVA 1.00	23.2
ELEVATOR	22.4	KVA	KVA	KVA 22.4	KVA 0.80	17.9
		KVA	KVA	KVA		KVA
		KVA	KVA	KVA		KVA
		KVA	KVA	KVA		KVA
		KVA	KVA	KVA		KVA
		KVA	KVA	KVA		KVA
		KVA	KVA	KVA		KVA
TOTALS (CONN. KVA)	45.9	KVA 333.8	KVA	KVA 379.8	KVA	331.9
TOTALS (CONN. KVA + 20%)	55.1	KVA 400.6	KVA	KVA 455.7	KVA	398.2
TOTALS (CONN. AMPS)	127.5	AMPS 926.6	AMPS	AMPS 1054.4	AMPS	921.2
TOTALS (CONN. AMPS + 20%)	153.0	AMPS 1112.0	AMPS	AMPS 1265.0	AMPS	1105.4

11/20/2025 8:36:54 AM
C:\Users\Brian.Pacansky\Documents\BLOG\1075-1625040-E_Brian.Pacansky\QDKV.E.rvt



EP701

D


C

B

A

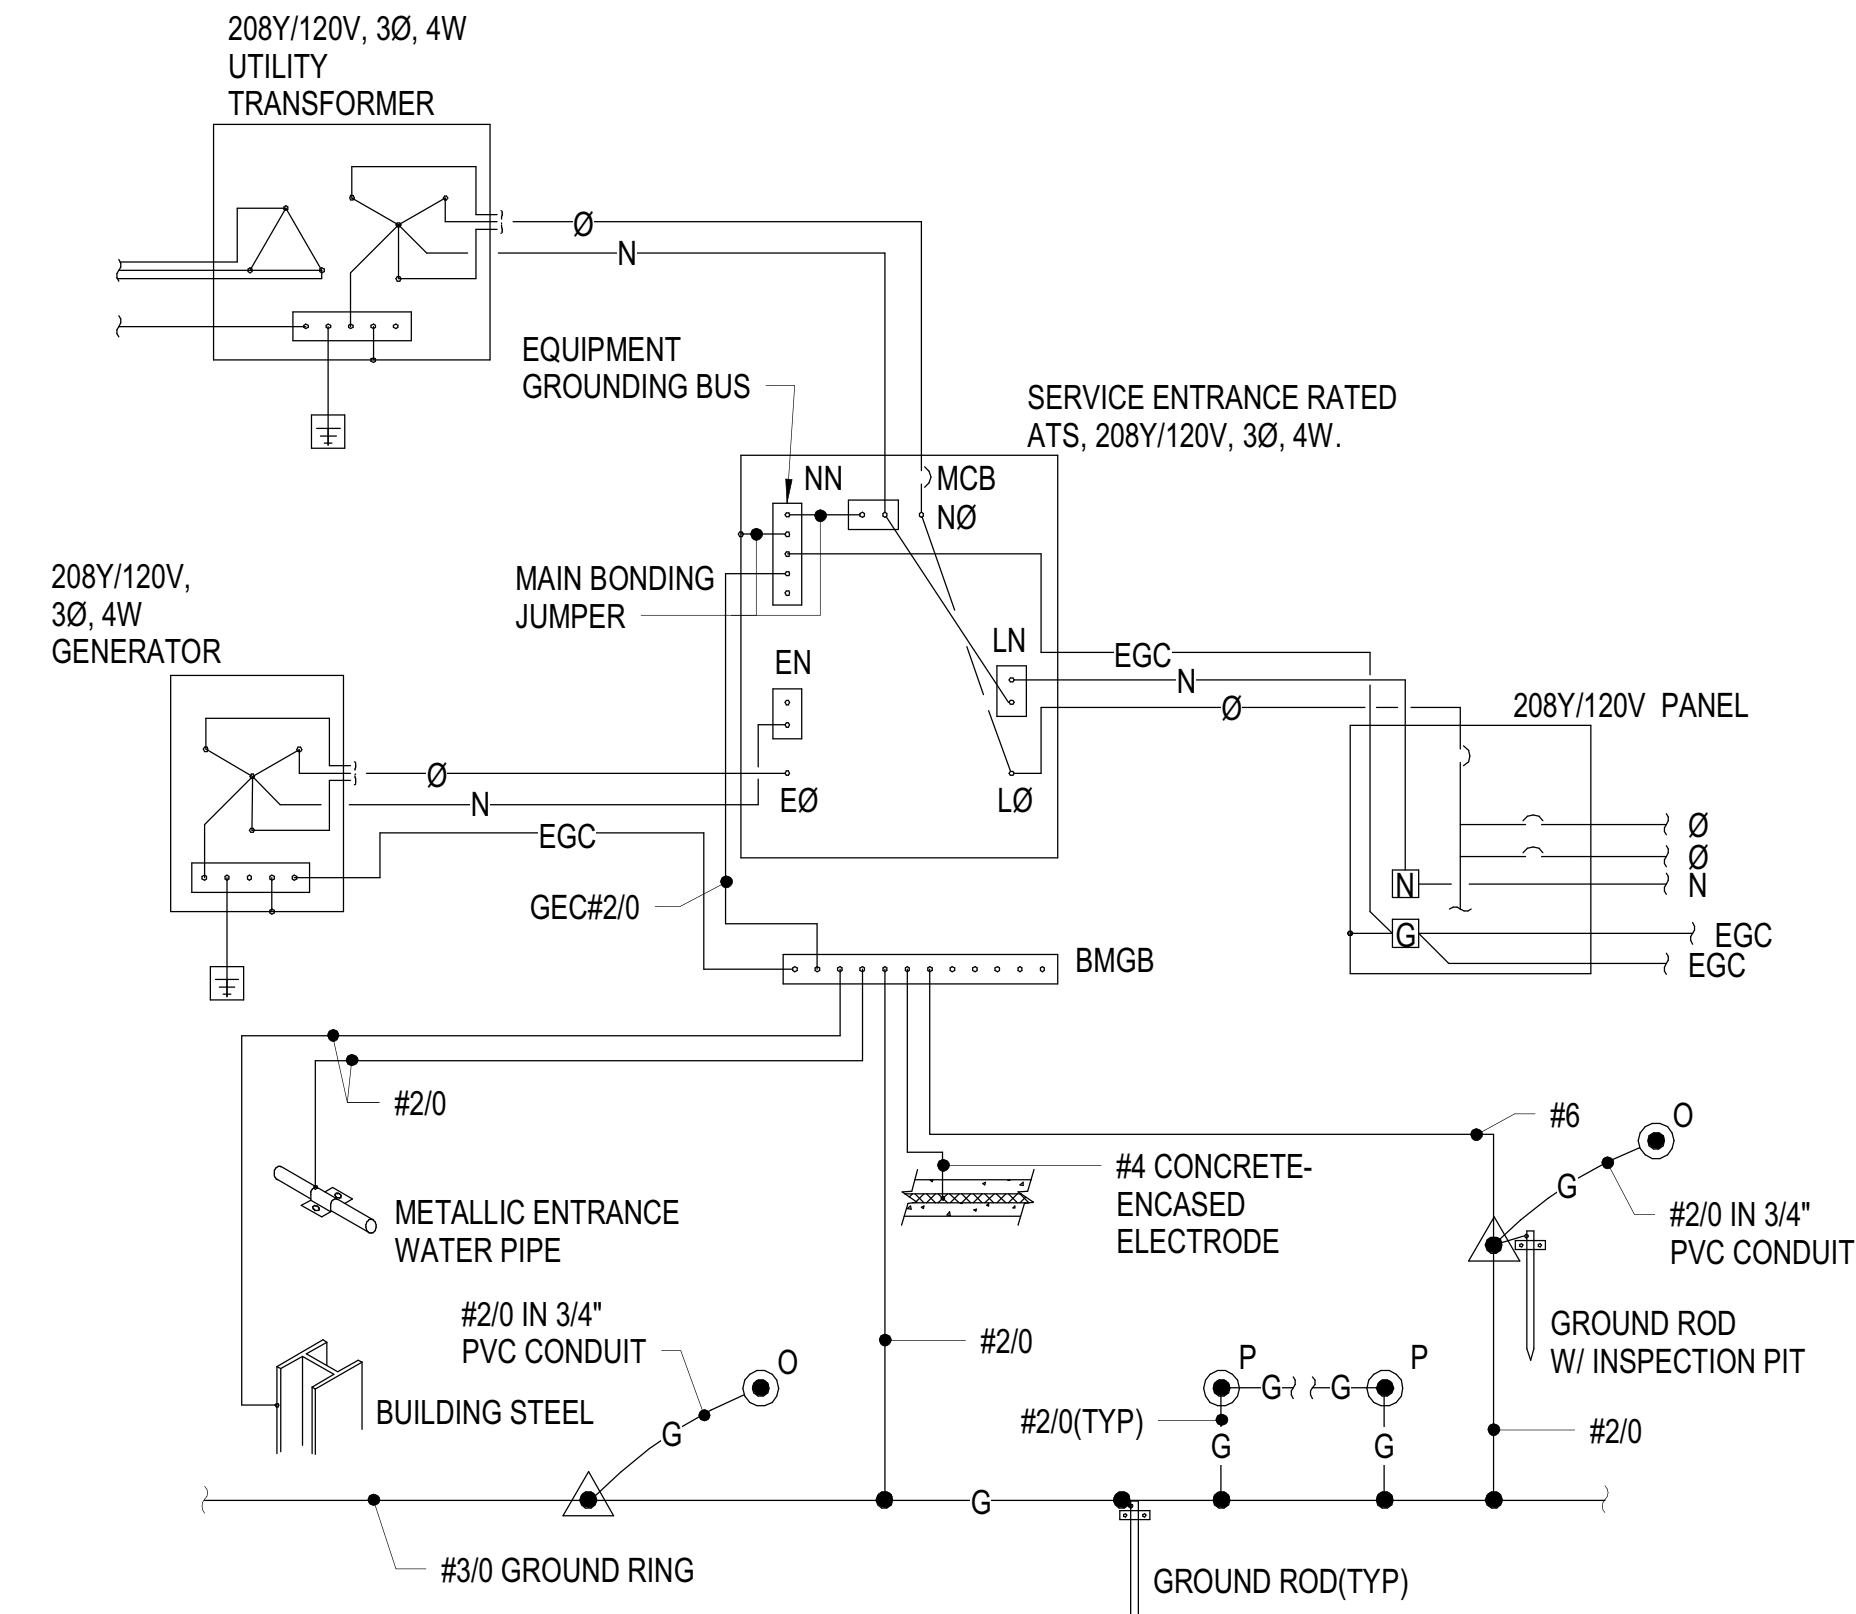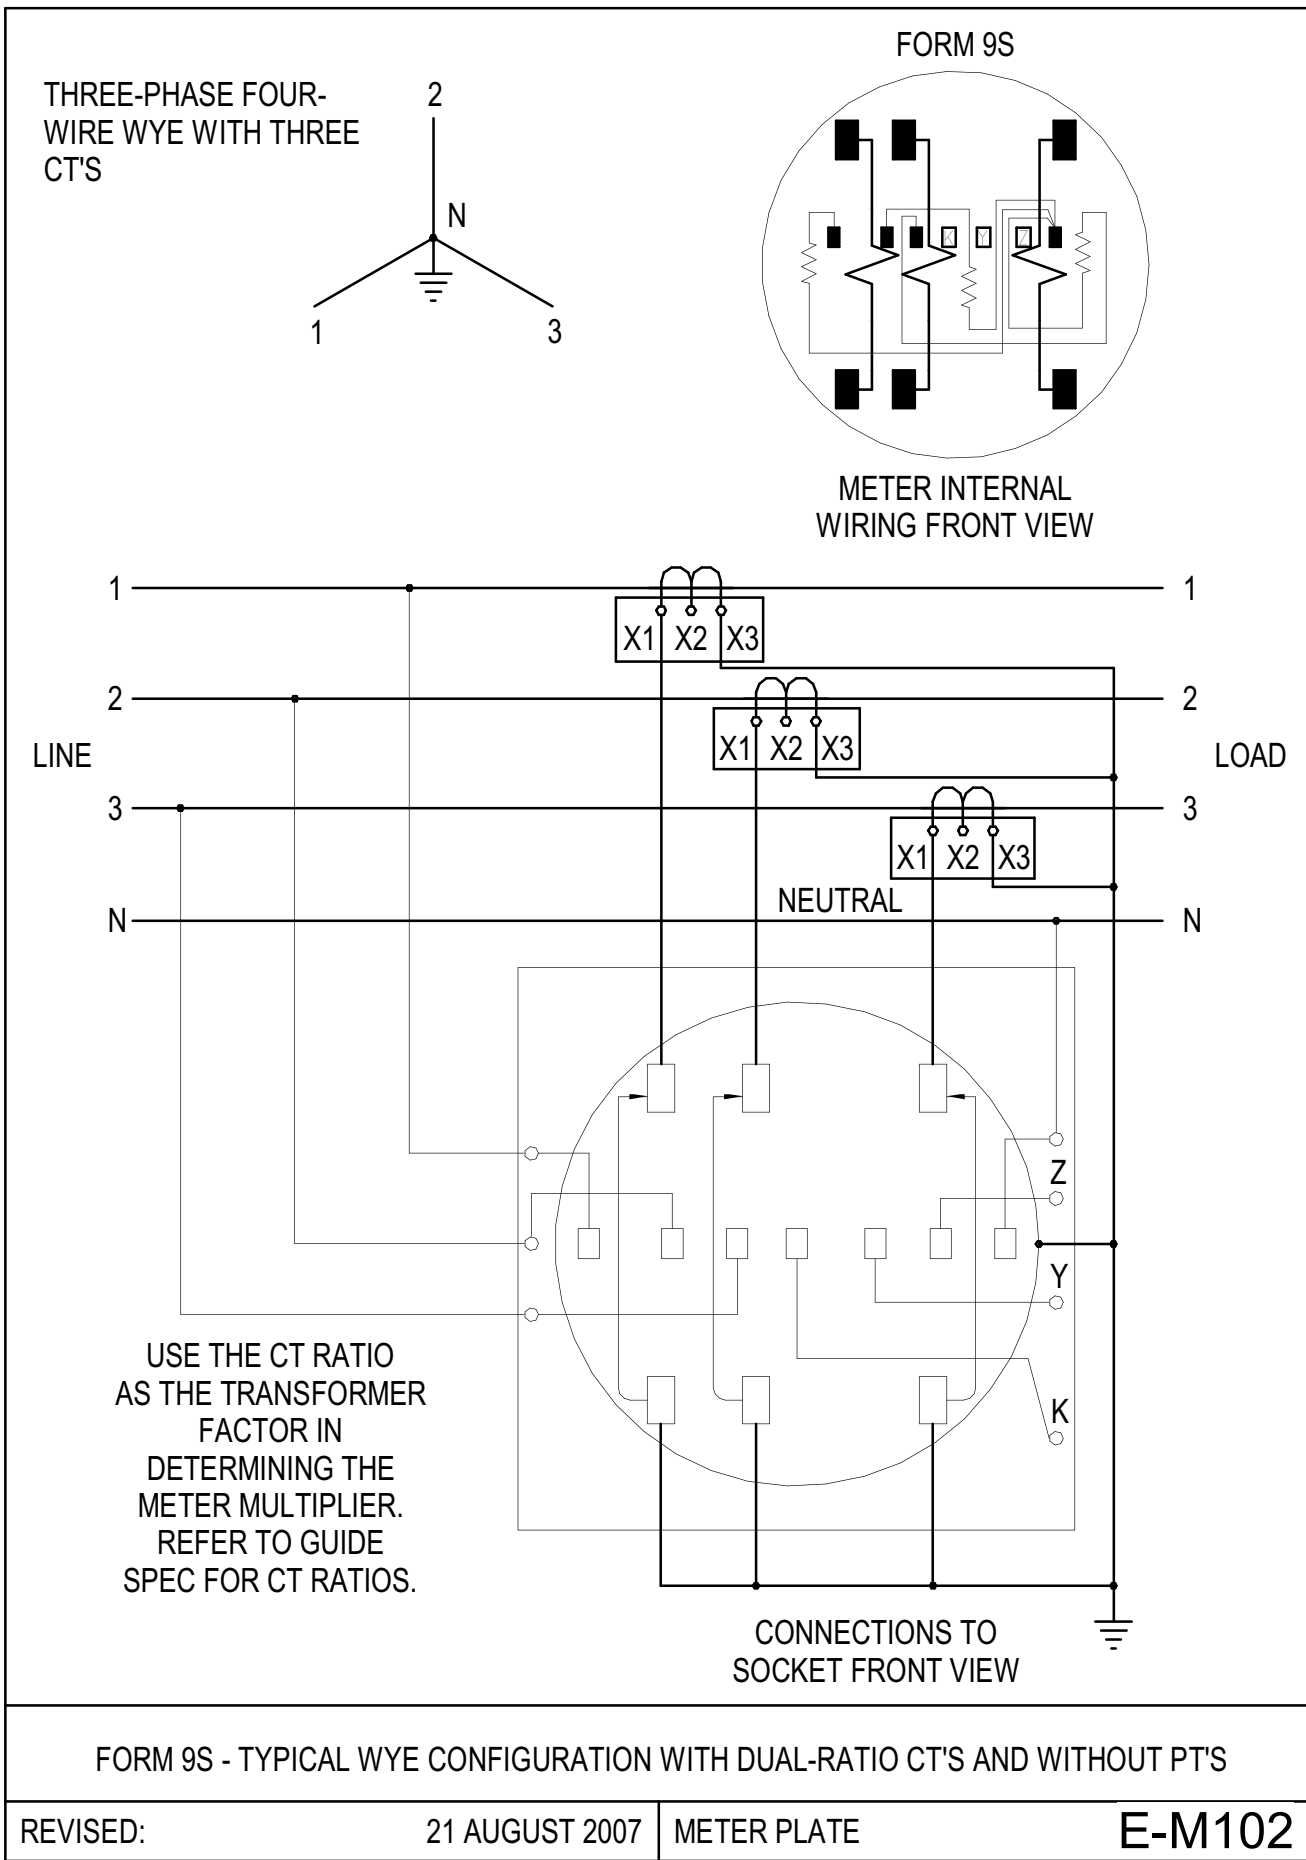

A1 SERVICE GROUNDING DIAGRAM
NOT TO SCALE

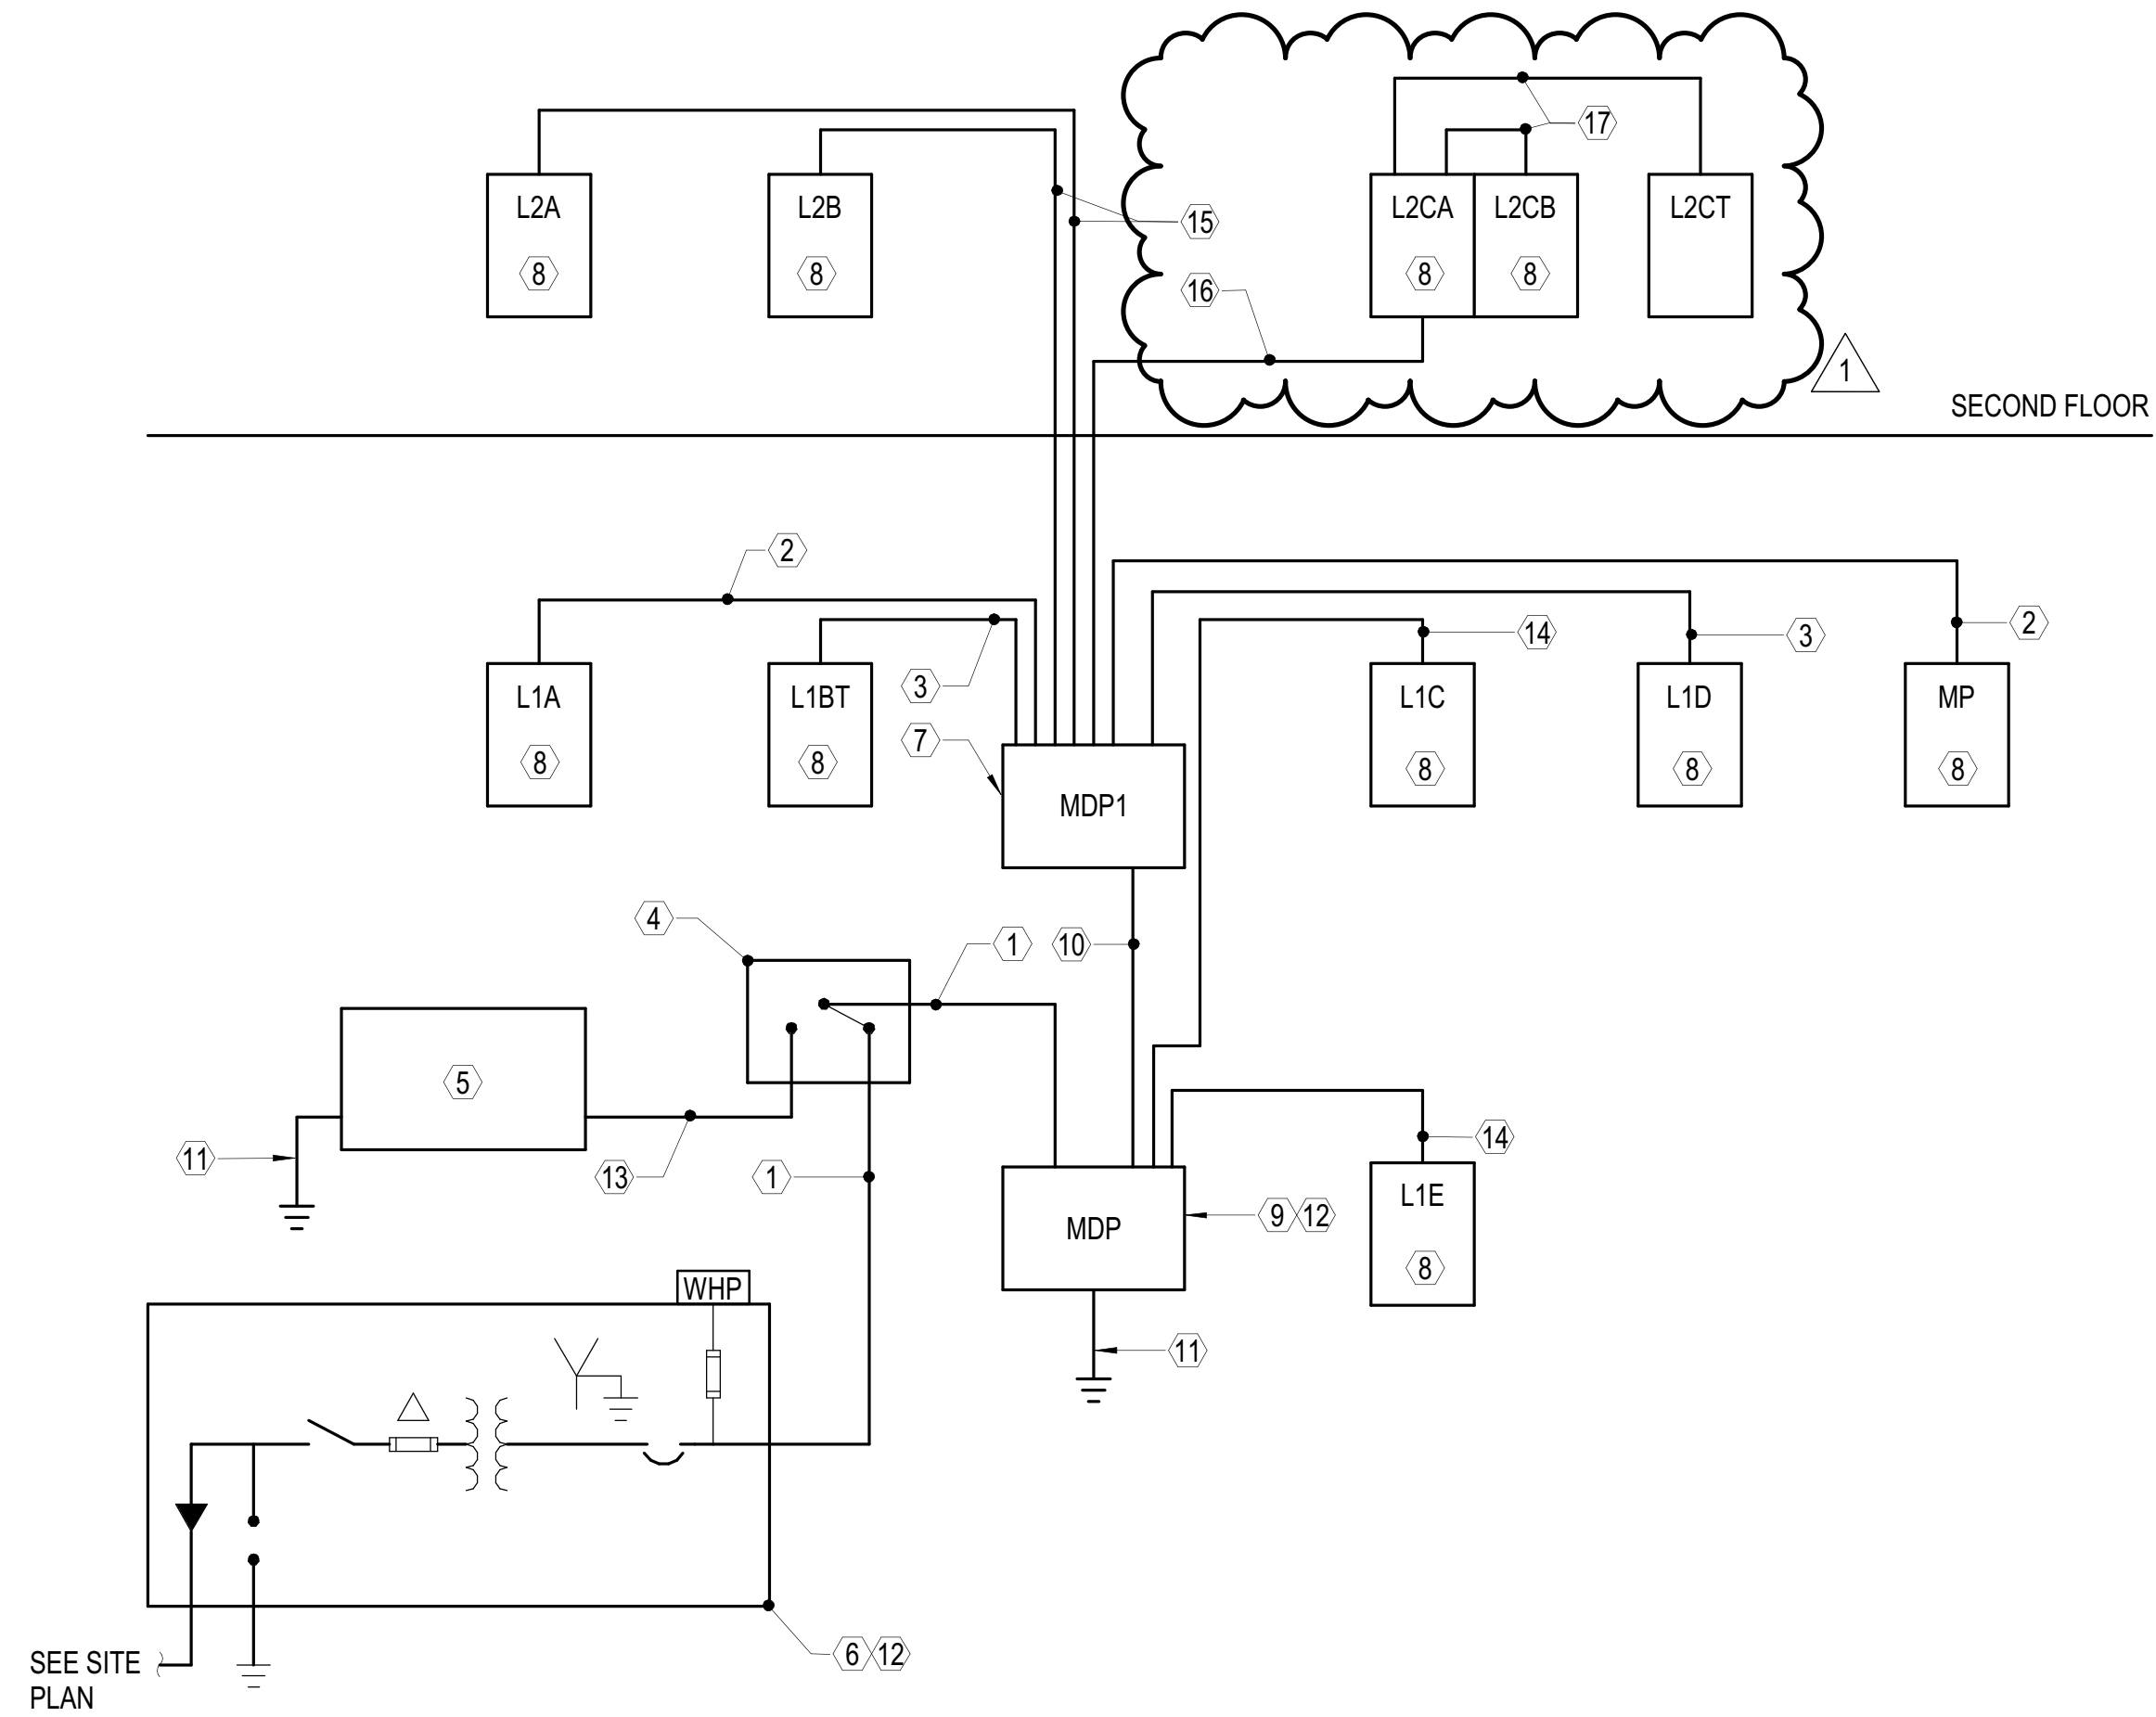

A2 POWER RISER DIAGRAM
NOT TO SCALE

GENERAL SHEET NOTES

SHEET KEYNOTES

- 1 PROVIDE 5 SETS 4-600 KCML, 1#3/0 GND, 4" CONCRETE ENCASED DUCTBANK. PROVIDE 6 WAY DUCTBANK.
- 2 PROVIDE 4#4/0, 1#4 GND IN EXISTING 3"C.
- 3 PROVIDE 4#1, 1#6 GND, 1#6 GND IN EXISTING 1-1/2"C.
- 4 PROVIDE 2000A, 4P, 208V SERVICE ENTRANCE RATED AUTOMATIC TRANSFER SWITCH.
- 5 RELOCATED 300KW/375KVA, 208Y/120V, 3Ø DIESEL GENERATOR.
- 6 PROVIDE 500KVA, 34500-208Y/120V, 3Ø, LIQUID FILLED, PAD MOUNTED TRANSFORMER.
- 7 PROVIDE PANELBOARD MDP1, 1200A MLO 208Y/120V, 3Ø.
- 8 PROVIDE 225A MLO, 208Y/120V, 3Ø, PANELBOARD.
- 9 PROVIDE SWITCHBOARD MDP 2000A MCB, 208Y/120V, 3Ø, 4W.
- 10 3 SETS OF 3-600 KCML, 1-600 KCML(N), 350 KCML (G), IN 4" CONDUITS.
- 11 PROVIDE #3/0 GROUND.
- 12 PROVIDE NEW TRANSFORMER AND MDP AS INDICATED TO MINIMIZE THE AMOUNT OF TIME THAT THE BUILDING IS WITHOUT POWER.
- 13 PROVIDE 3 SETS 4-600 KCML, 1#3/0 GND, 4" CONCRETE ENCASED DUCTBANK. PROVIDE 4 WAY DUCTBANK.
- 14 PROVIDE 4#4/0, 1#4 GND IN 2 1/2"C.
- 15 PROVIDE 4#1/0, 1#6 GND IN EXISTING 1-1/2"C.
- 16 PROVIDE 4-350 KCML, 1#4 GND IN EXISTING 3"C.
- 17 PROVIDE 4#1, 1#6 GND IN 1-1/2"C.

DATE	SYN	DESCRIPTION	APPR
11/2/05	1	CONSOLIDATED REVISIONS	



CLARK NEXSEN
A JMET Company
4525 MAIN STREET
SUITE 1400
VIRGINIA BEACH, VA 23462
757-455-5800 FAX 757-455-5638
WWW.CLARKNEXSEN.COM

APPROVED	AE INFO
FOR COMMANDER NAVFAC	
ACTIVITY	Approved by Don Bryant, PE, N10
Facilities Engineer, NSWDC	
via Email	
SATISFACTORY TO DATE	07/09/2025
DES	BSP
DRW	MSW
CHK	SPS
PMDW	JT/SW
BRANCH MANAGER	WRB
CHIEF ENGINEER	JW/J
FIRE PROTECTION	HPN

DEPARTMENT OF THE NAVY
NAVAL FACILITIES ENGINEERING SYSTEMS COMMAND
NAVAL FACILITIES ENGINEERING SYSTEMS COMMAND - MID-ATLANTIC
NAVAL STATION - NORFOLK, VA
NAS OCEANA, DAM NECK ANNEX
Q-1075 SOF OPERATIONS BUILDING ADDITION
VIRGINIA BEACH, VA
POWER RISER DIAGRAMS

SCALE	AS NOTED
PROJECT NO.	1625040
CONSTR. CONTR. NO.	N40085-19-D-9041
NAVFAC DRAWING NO.	12929101
SHEET	196 OF 239
EP701	

DRAWFORM REVISION: 25 AUGUST 2020