

1

2


3

UNCLASSIFIED


4

5


D

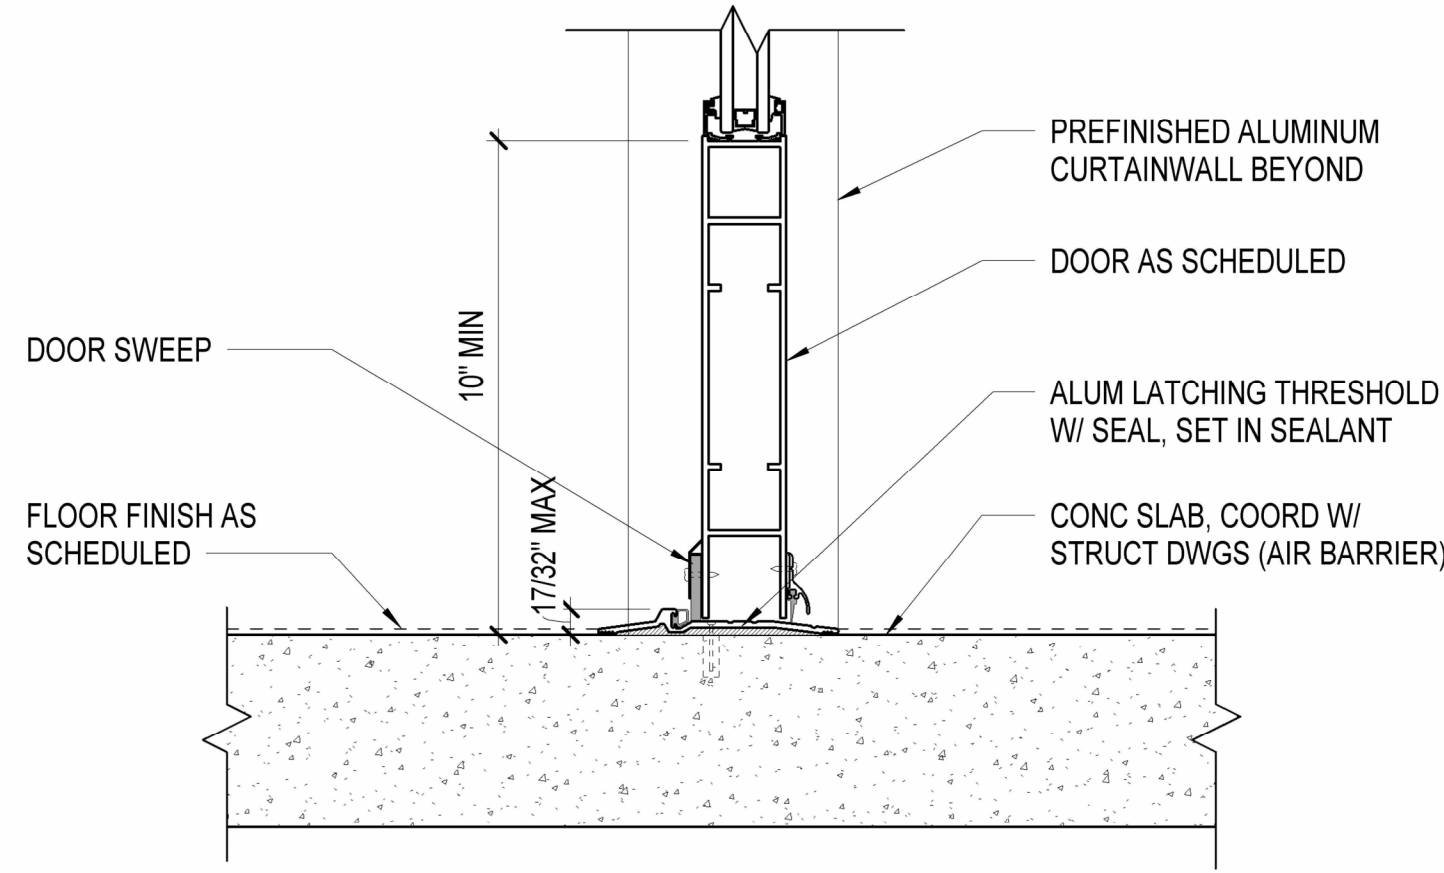

C1 SILL DETAIL
3" = 1'-0" AT ENTRY STOREFRONT

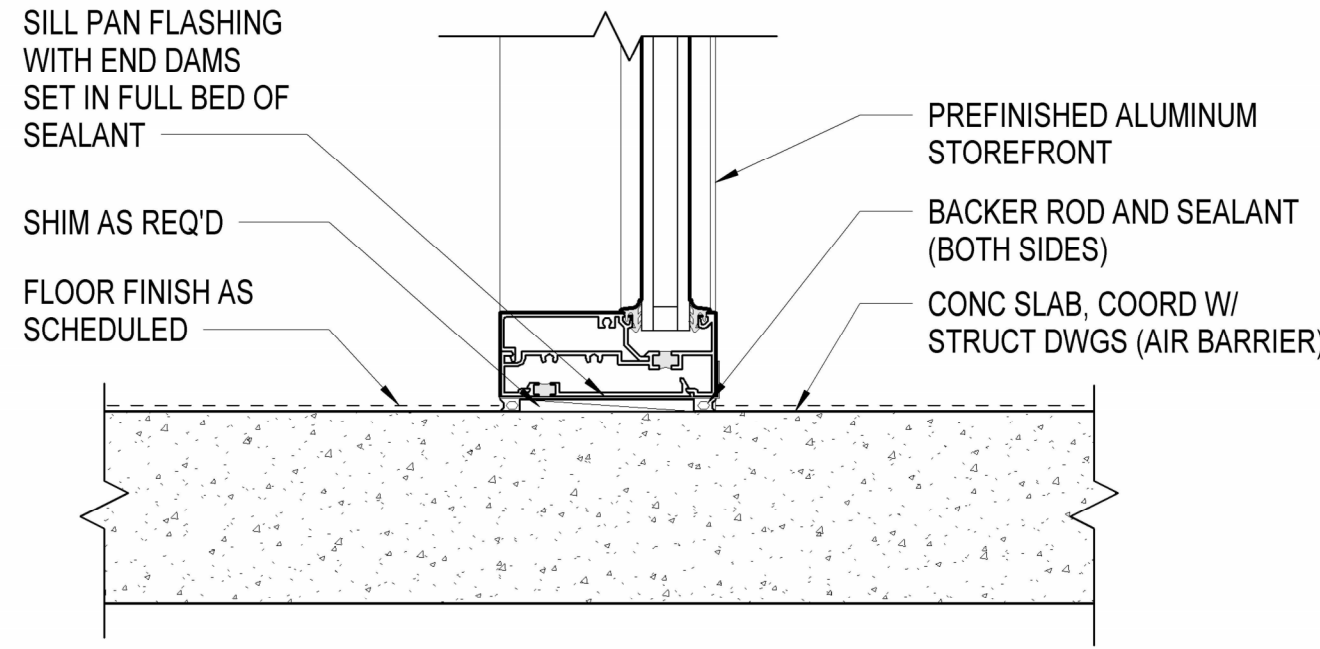


C2 SILL DETAIL
3" = 1'-0" AT ENTRY STOREFRONT

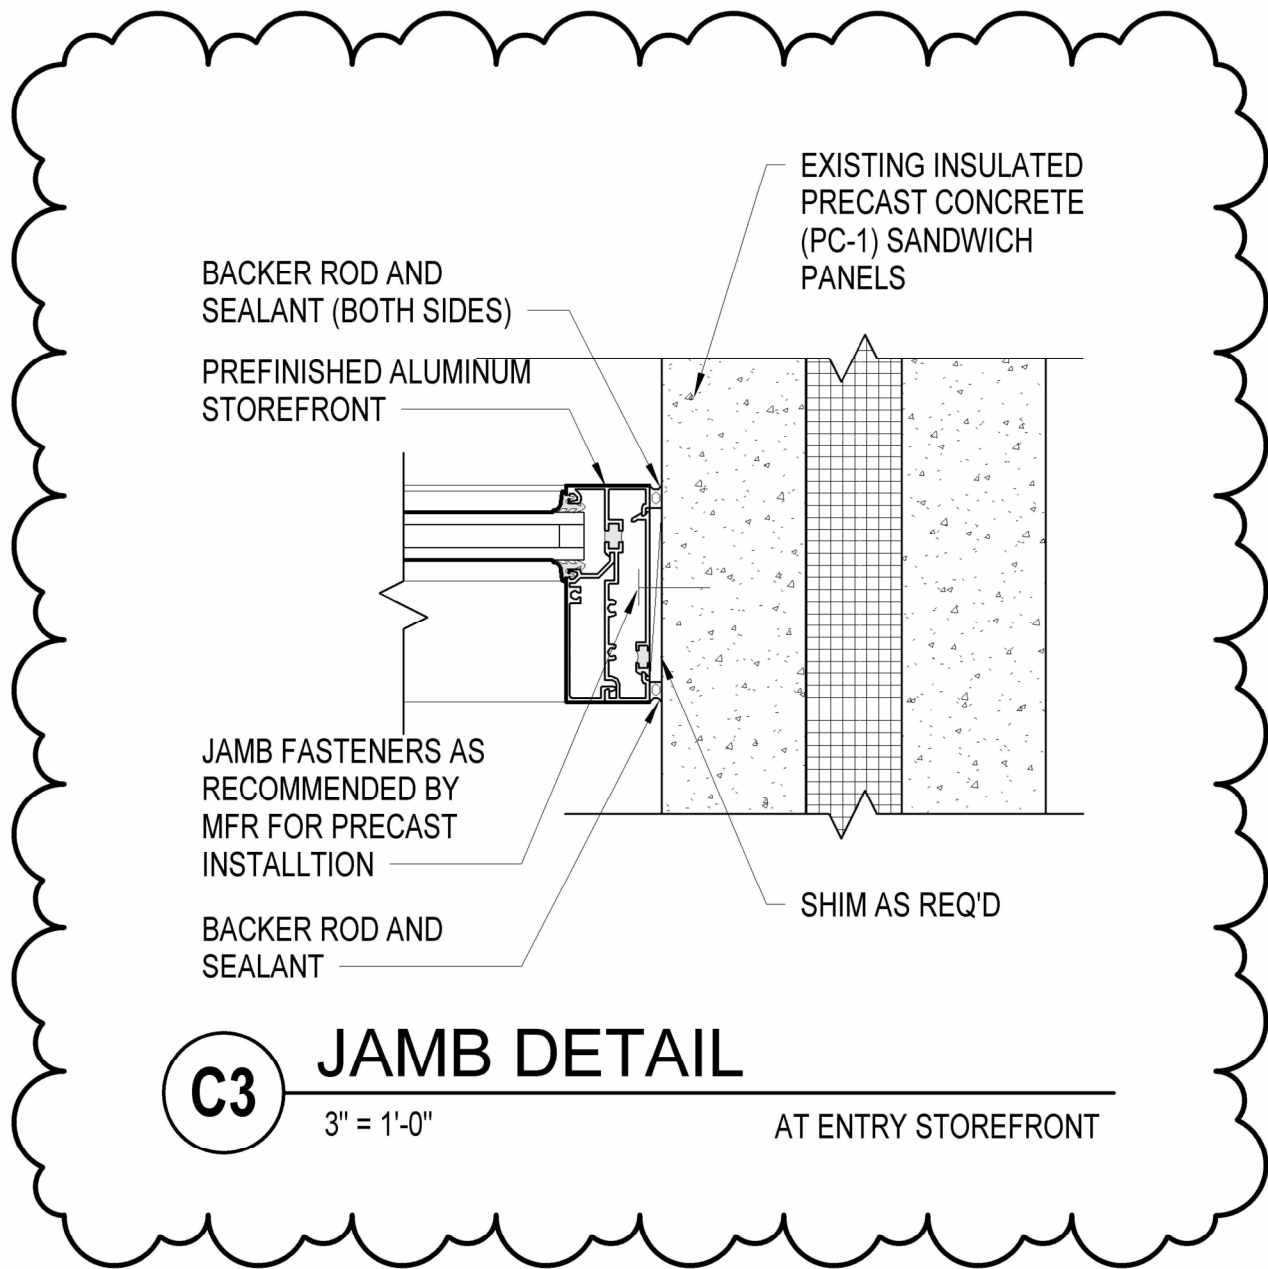


C3 JAMB DETAIL
3" = 1'-0" AT ENTRY STOREFRONT

C

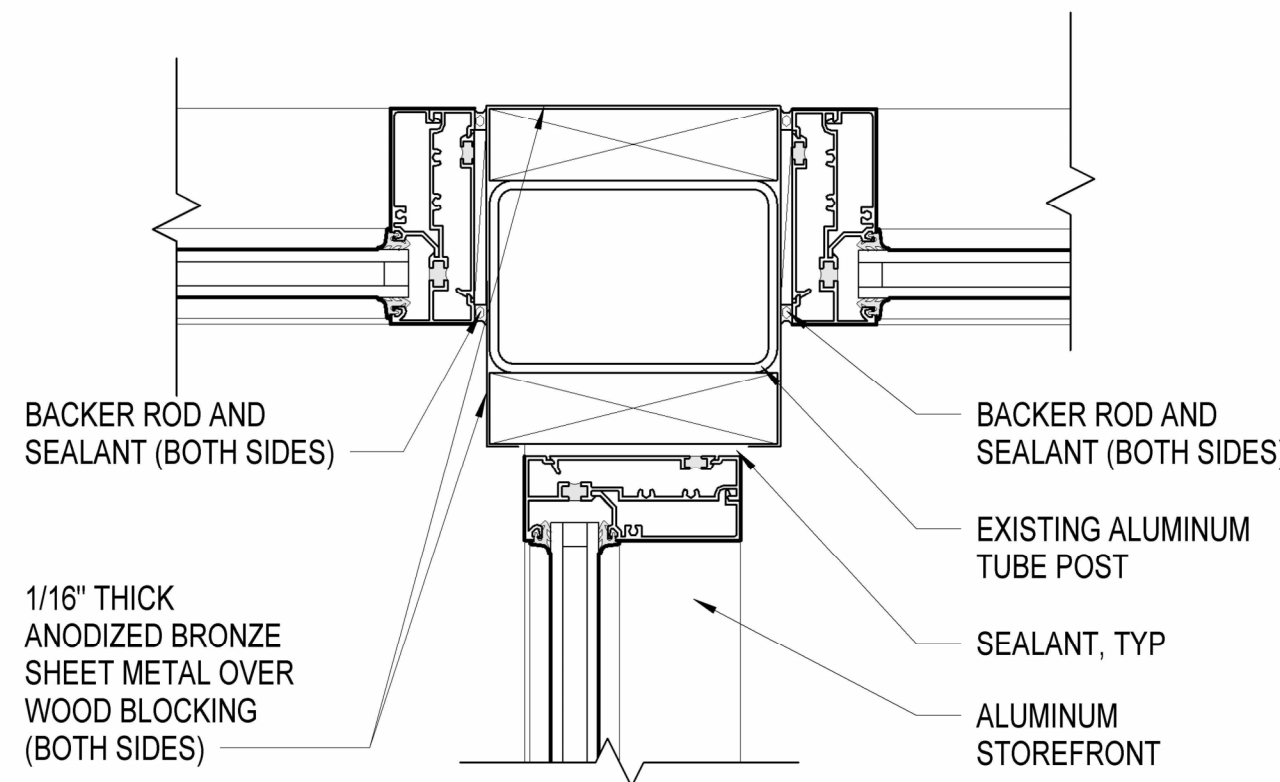


B1 STOREFRONT CORNER DETAIL
3" = 1'-0" AT ENTRY STOREFRONT

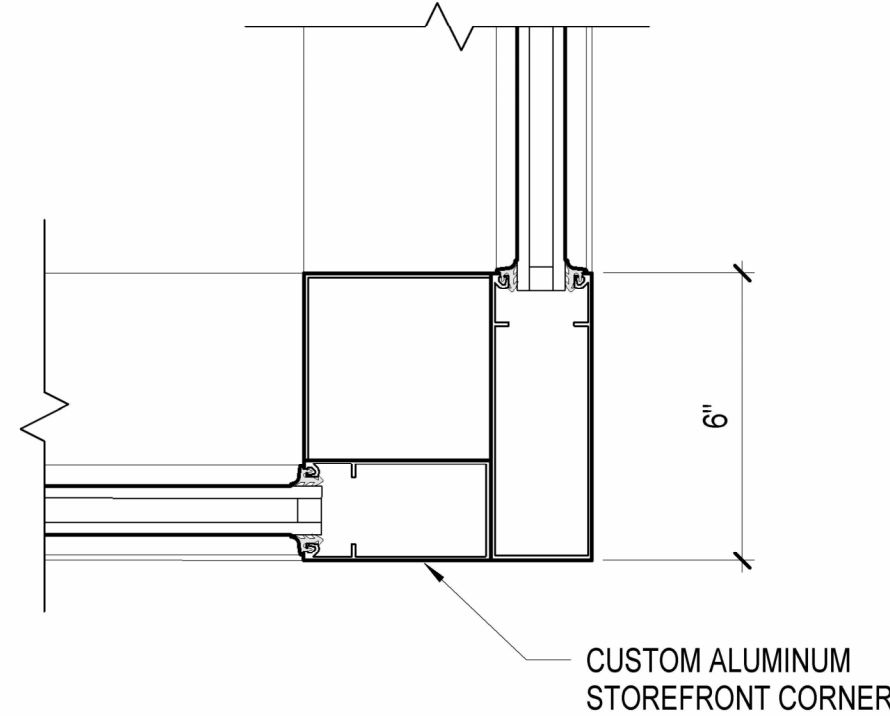


B2 STOREFRONT CORNER DETAIL
3" = 1'-0" AT ENTRY STOREFRONT


B

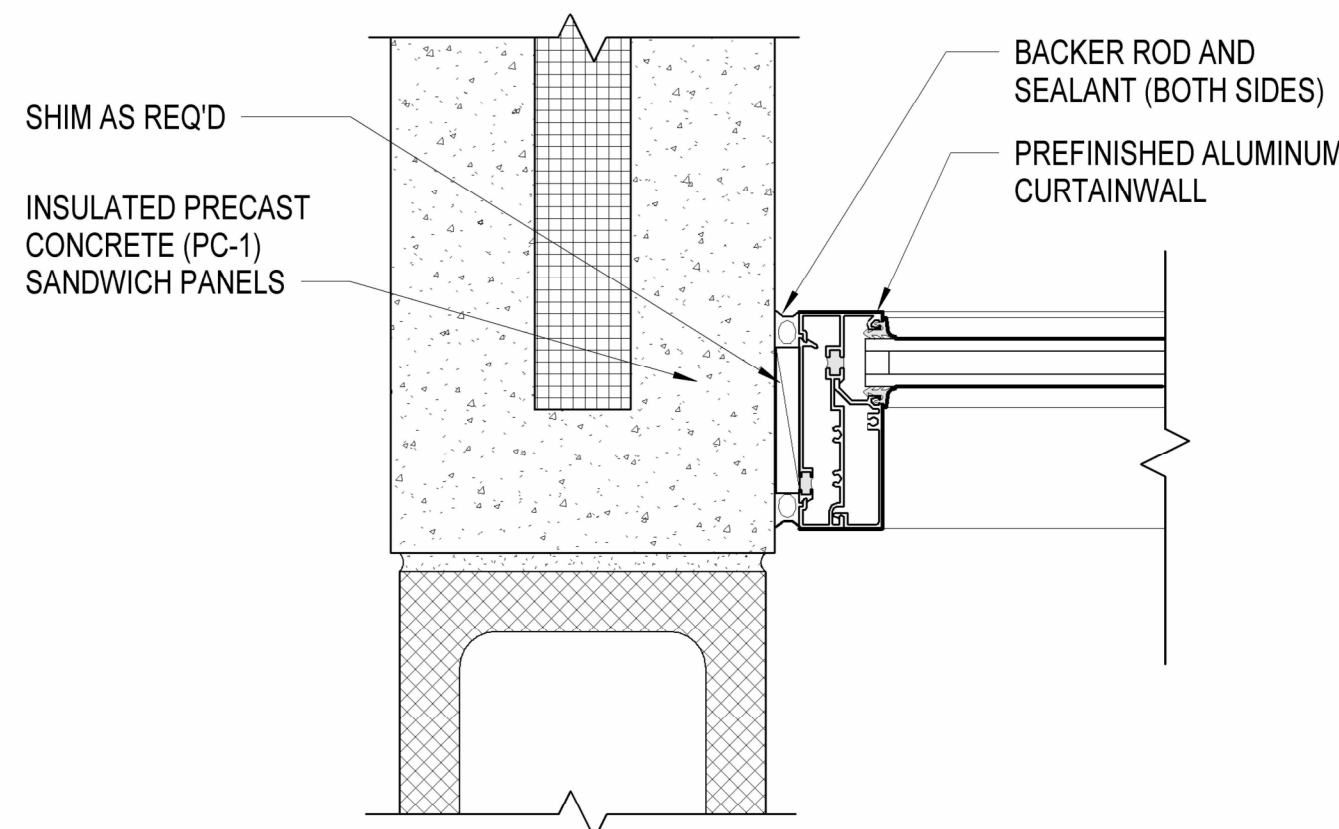

A1 JAMB DETAIL
3" = 1'-0" AT ENTRY STOREFRONT

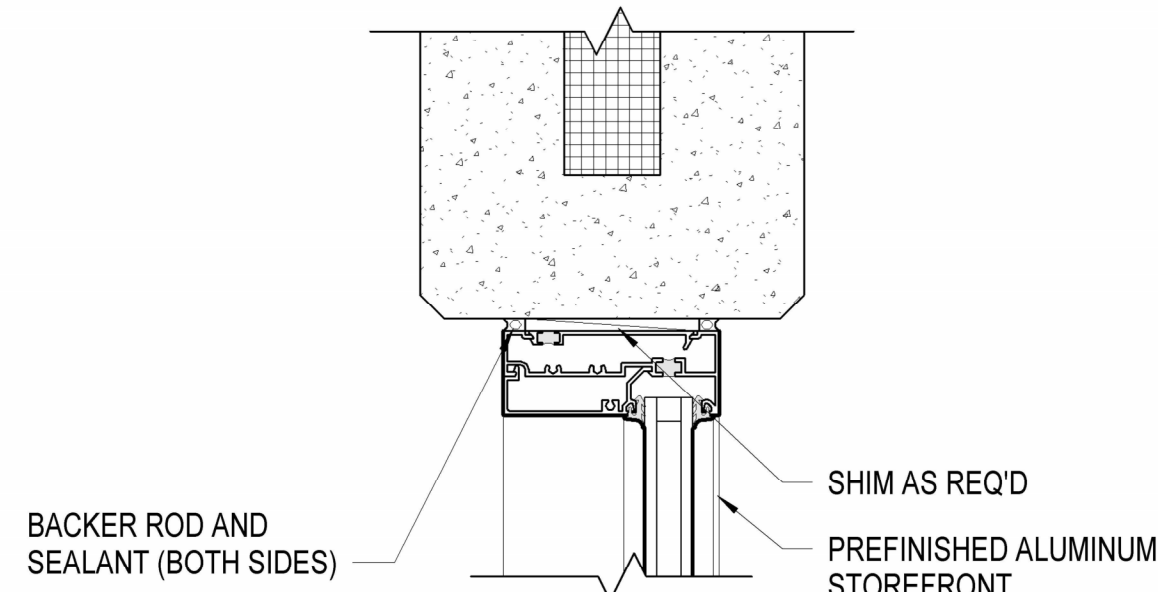


A2 HEAD DETAIL
3" = 1'-0" AT ENTRY STOREFRONT

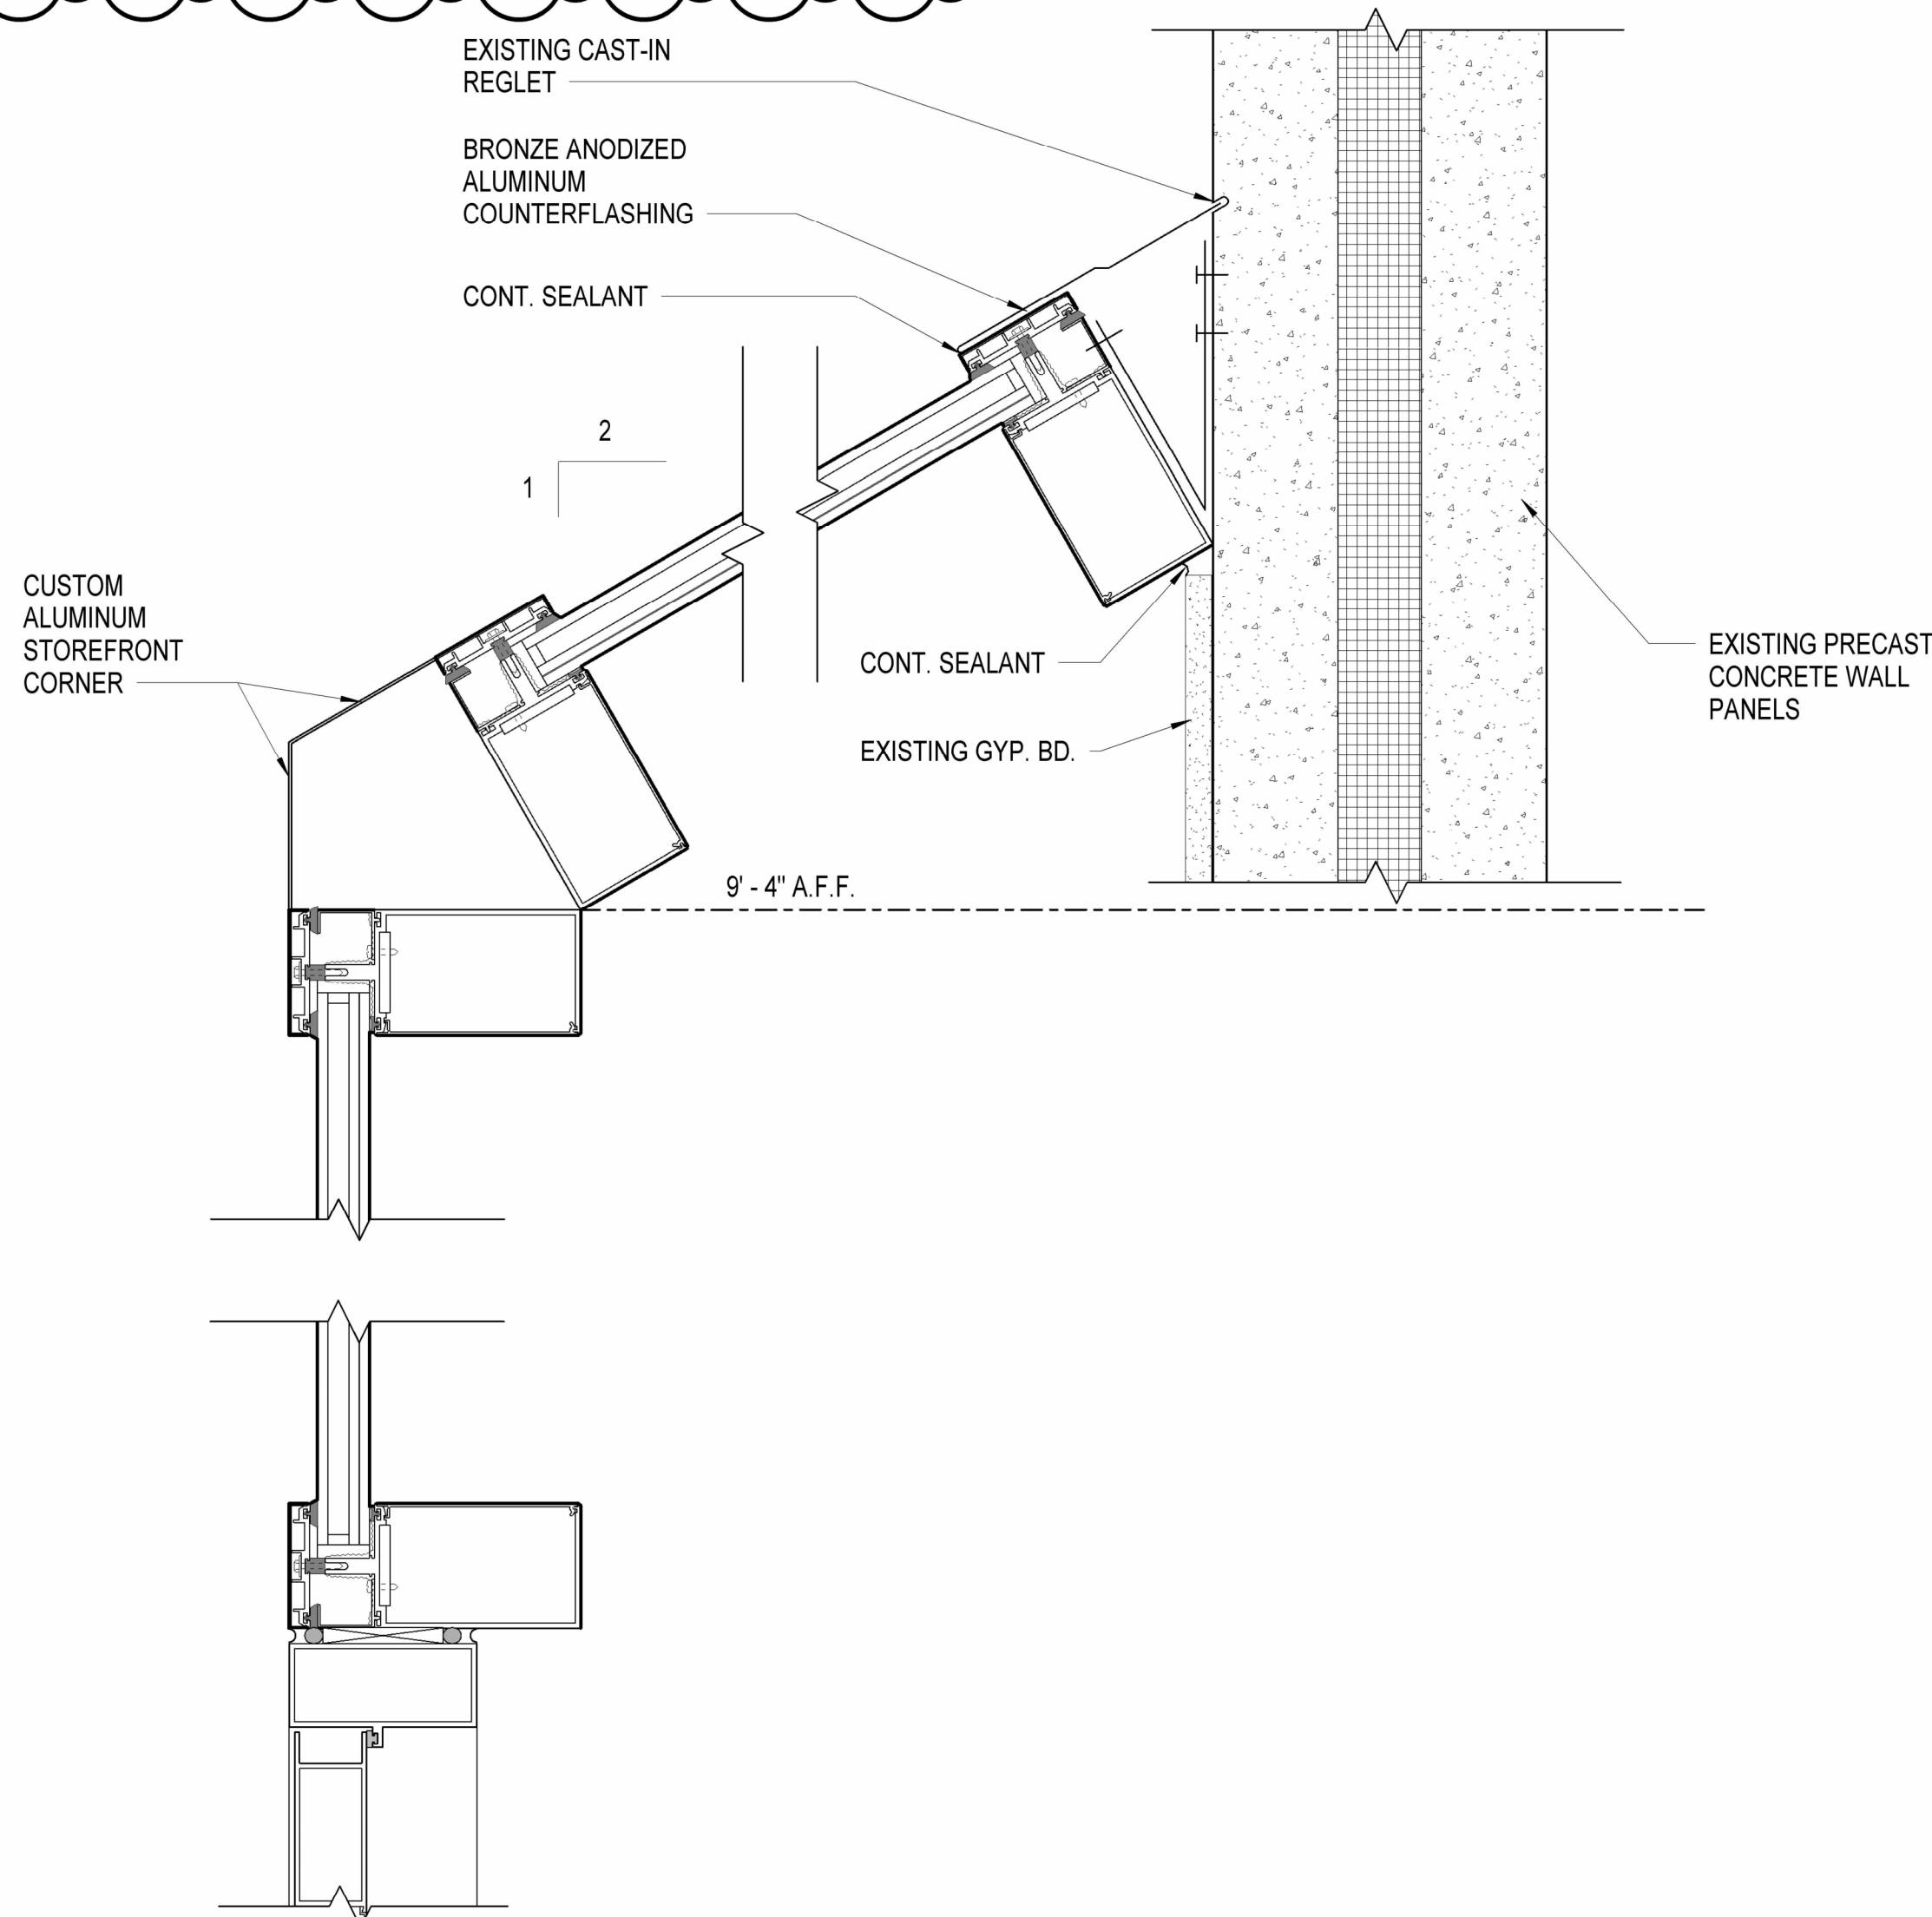

A3 STOREFRONT HEAD DETAIL
3" = 1'-0" AT ENTRY STOREFRONT

GRAPHIC SCALE(S)

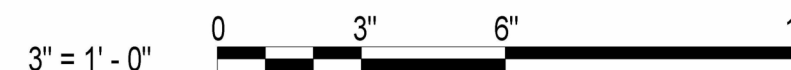

D

C

UNCLASSIFIED

B

A

DATE	SYN	DESCRIPTION	APPR
12/02/25	2	CONSOLIDATED REVISIONS	



CLARKNEXSEN
A JMET Company
4525 MAIN STREET SUITE 1400
VIRGINIA BEACH, VA 23462
757-455-5800 FAX 757-455-5638
WWW.CLARKNEXSEN.COM

APPROVED	AE INFO
FOR COMMANDER NAVFAC	
ACTIVITY	Approved by Don Bryant, PE, N10 Facilities Engineer, NSWDG via Email
SATISFACTORY TO DATE	07/09/2025
DES	DJH
BRW	SAB
CHK	RAM
PMOM	JT/SW
BRANCH MANAGER	DJD
CHIEF ENGINEER	JWJ
FIRE PROTECTION	HPN

DEPARTMENT OF THE NAVY	NAVAL FACILITIES ENGINEERING SYSTEMS COMMAND
NAVAL FACILITIES ENGINEERING SYSTEMS COMMAND - MID-ATLANTIC	NAVAL STATION - NORFOLK, VA
NAS OCEANA, DAM NECK ANNEX	VIRGINIA BEACH, VA
Q-1075 SOF OPERATIONS BUILDING ADDITION	
CURTAIN WALL & STOREFRONT DETAILS	

SCALE: AS NOTED
PROJECT NO.: 1625040
CONSTR. CONTR. NO. N40085-19-D-9041
NAVFAC DRAWING NO. 12929003
SHEET 98 OF 239
AE704

DRAWING REVISION: 25 AUGUST 2020

1

2

3

UNCLASSIFIED

4

5