

1

2

3

UNCLASSIFIED

4


5

D


C

B


A

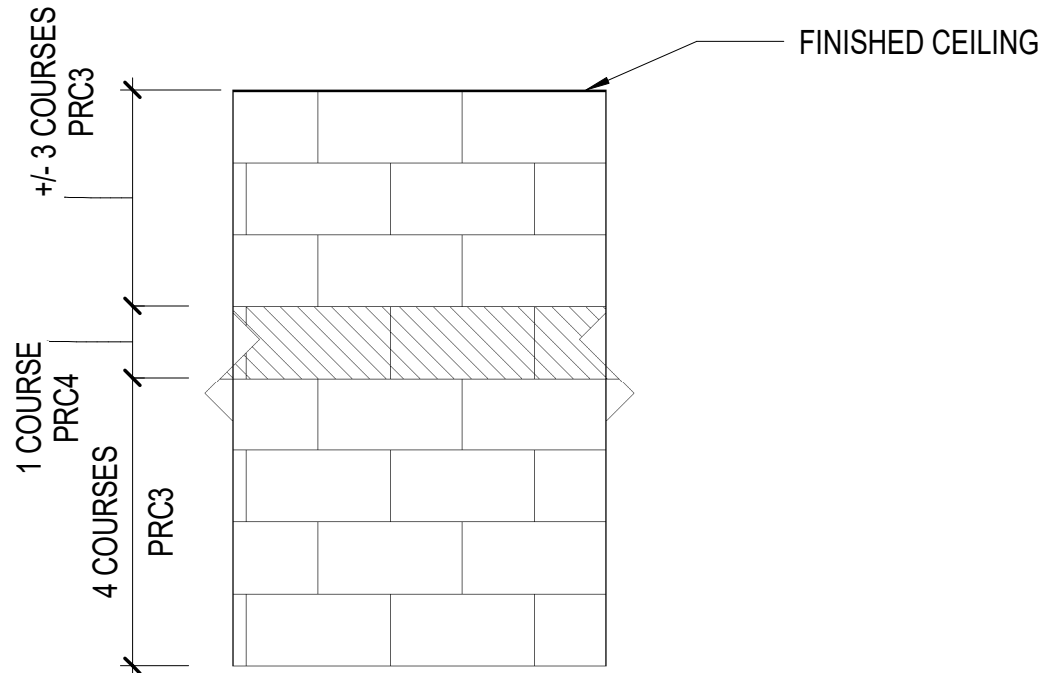

D1 WALL TILE ELEVATION TYP
3/8" = 1'-0"

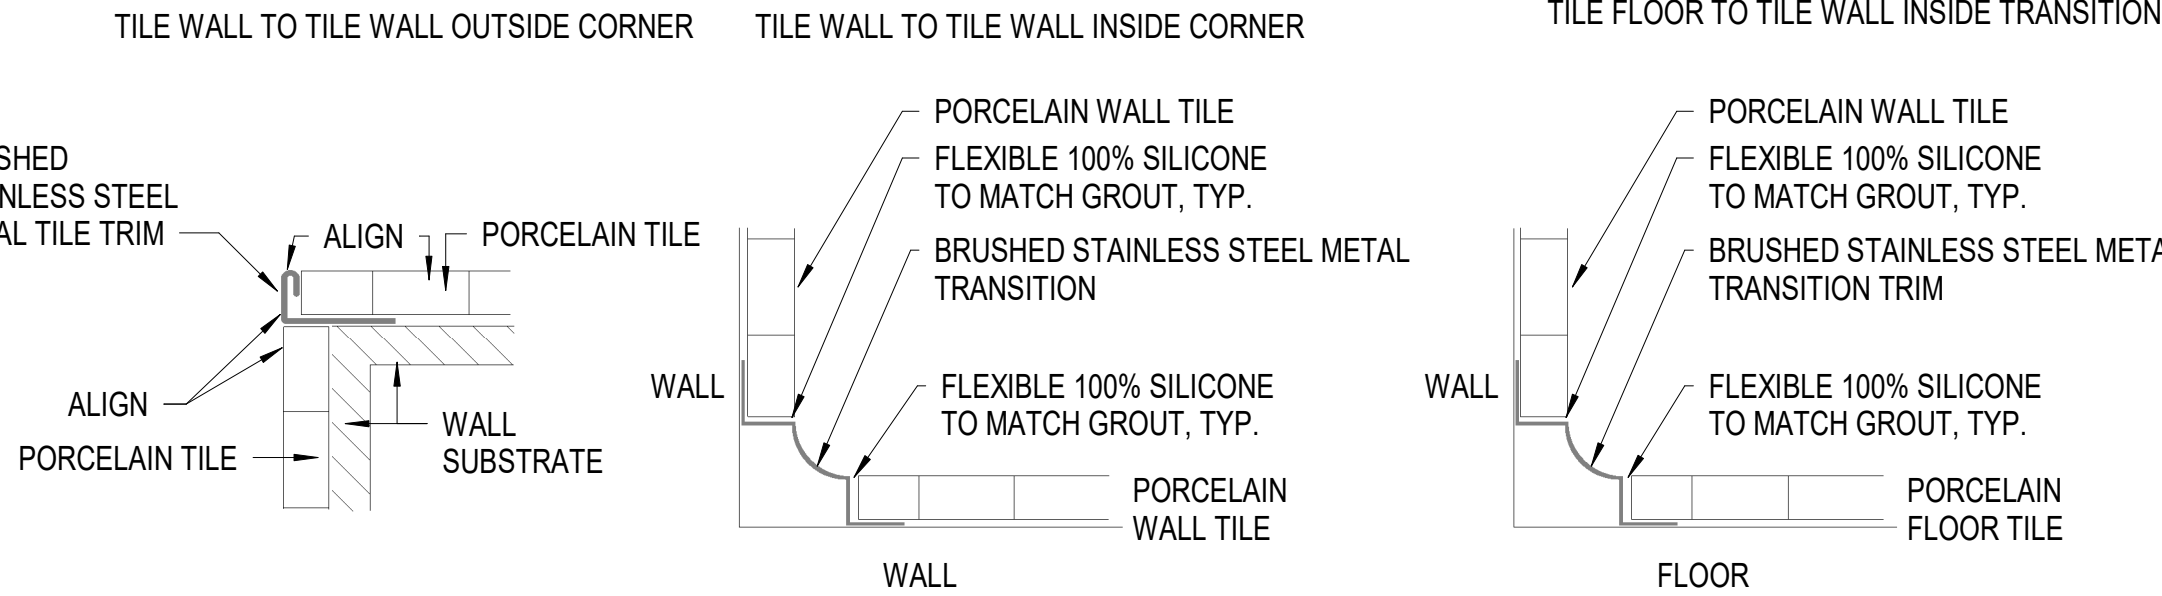

D2 FLOOR AND WALL TILE TRANSITIONS
1 1/2" = 1'-0"

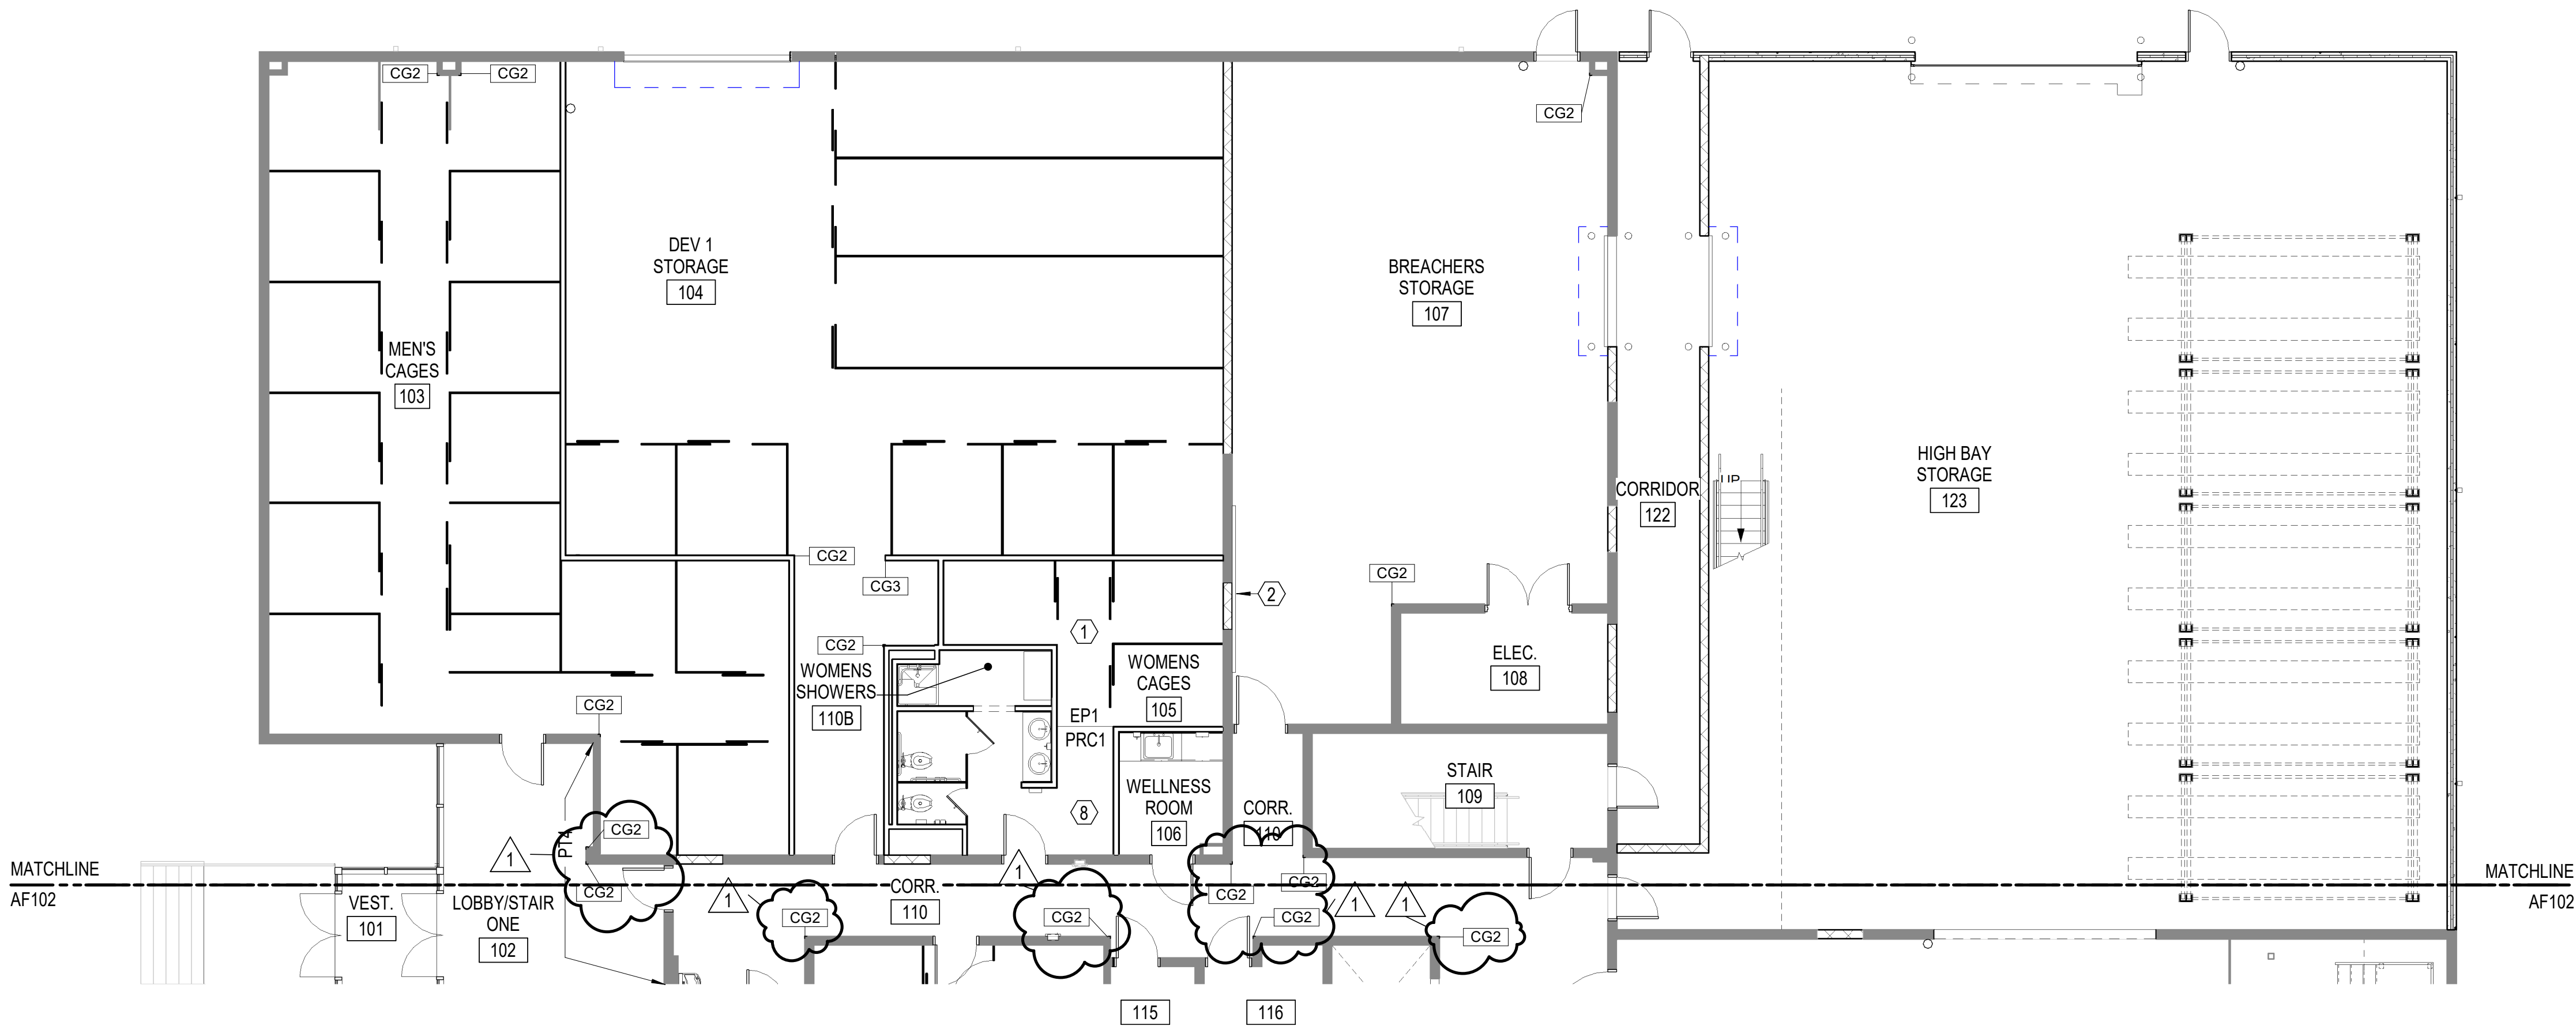

A1 FIRST FLOOR FINISH & SIGNAGE PLAN AREA A
1/8" = 1'-0"

GENERAL NOTES

1. REFER TO SHEET AG601 FOR SIGNAGE TYPES.
2. REFER TO SHEET AF601 FOR FINISH SCHEDULE AND LEGEND.
3. REFER TO SPECIFICATION SECTION 10 14 00.20 INTERIOR SIGNAGE FOR INTERIOR SIGNAGE SCHEDULE.

KEY NOTES

1. PROVIDE RUBBER WALL BASE AND PAINTED WALLS IN AREA OF EPOXY AS SCHEDULED.
2. PROVIDE 144"W X 48"H PORCELAIN MARKERBOARD WITH ALUMINUM FRAME AND ALUMINUM MARKER TRAY. BASIS OF DESIGN: GHENT. MOUNT WHITEBOARD 45" AFF TO BOTTOM.
8. PROVIDE FULL HEIGHT WALL TILE IN AREA OF TILED FLOOR.



CLARK NEXSEN
A JMT Company
4525 MAIN STREET
SUITE 1400
VIRGINIA BEACH, VA 23462
757-455-5800 FAX 757-455-5638
WWW.CLARKNEXSEN.COM

APPROVED

FOR COMMANDER NAVFAC

ACTIVITY
Approved by Don Bryant, PE, N10
Facilities Engineer, NSWDG
via Email

SATISFACTORY TO DATE 07/09/2025

DES RMM DRW RMM CHK SBD

PMOM JT/SW

BRANCH MANAGER DJD

CHIEF ENGINEER JWL

FIRE PROTECTION HPN

NAVAL FACILITIES ENGINEERING SYSTEMS COMMAND

NAVAL FACILITIES ENGINEERING SYSTEMS COMMAND - MID-ATLANTIC

NAVAL STATION - NORFOLK, VA

NAS OCEANA, DAM NECK ANNEX

Q-1075 SOF OPERATIONS BUILDING ADDITION


VIRGINIA BEACH, VA

FIRST FLOOR FINISH & SIGNAGE PLAN AREA A


SIGNAGE LEGEND

- ###
SIGNAGE SYMBOL CODED TO AG601

KEY PLAN

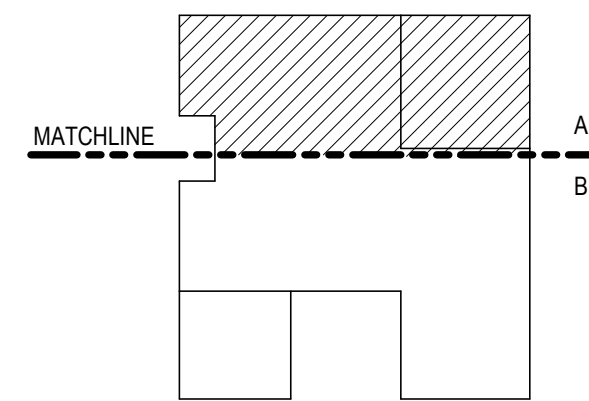

GRAPHIC SCALE(S)

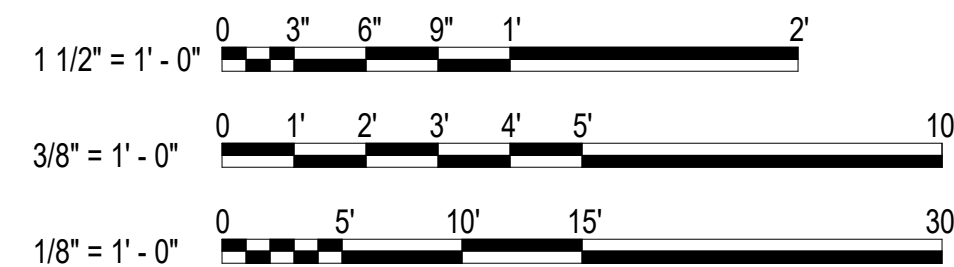

SCALE: AS NOTED

PROJECT NO.: 1625040

CONSTR. CONTR. NO.

N40085-19-D-9041

NAVFAC DRAWING NO.



12929006

SHEET 101 OF 239

AF101

DRAWING REVISION: 25 AUGUST 2020

11/19/2025 1:58:00 AM AF 102
C:\Revit\Projects\BLDG\075-1625000-A_Relaym_Mater.rvt

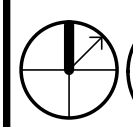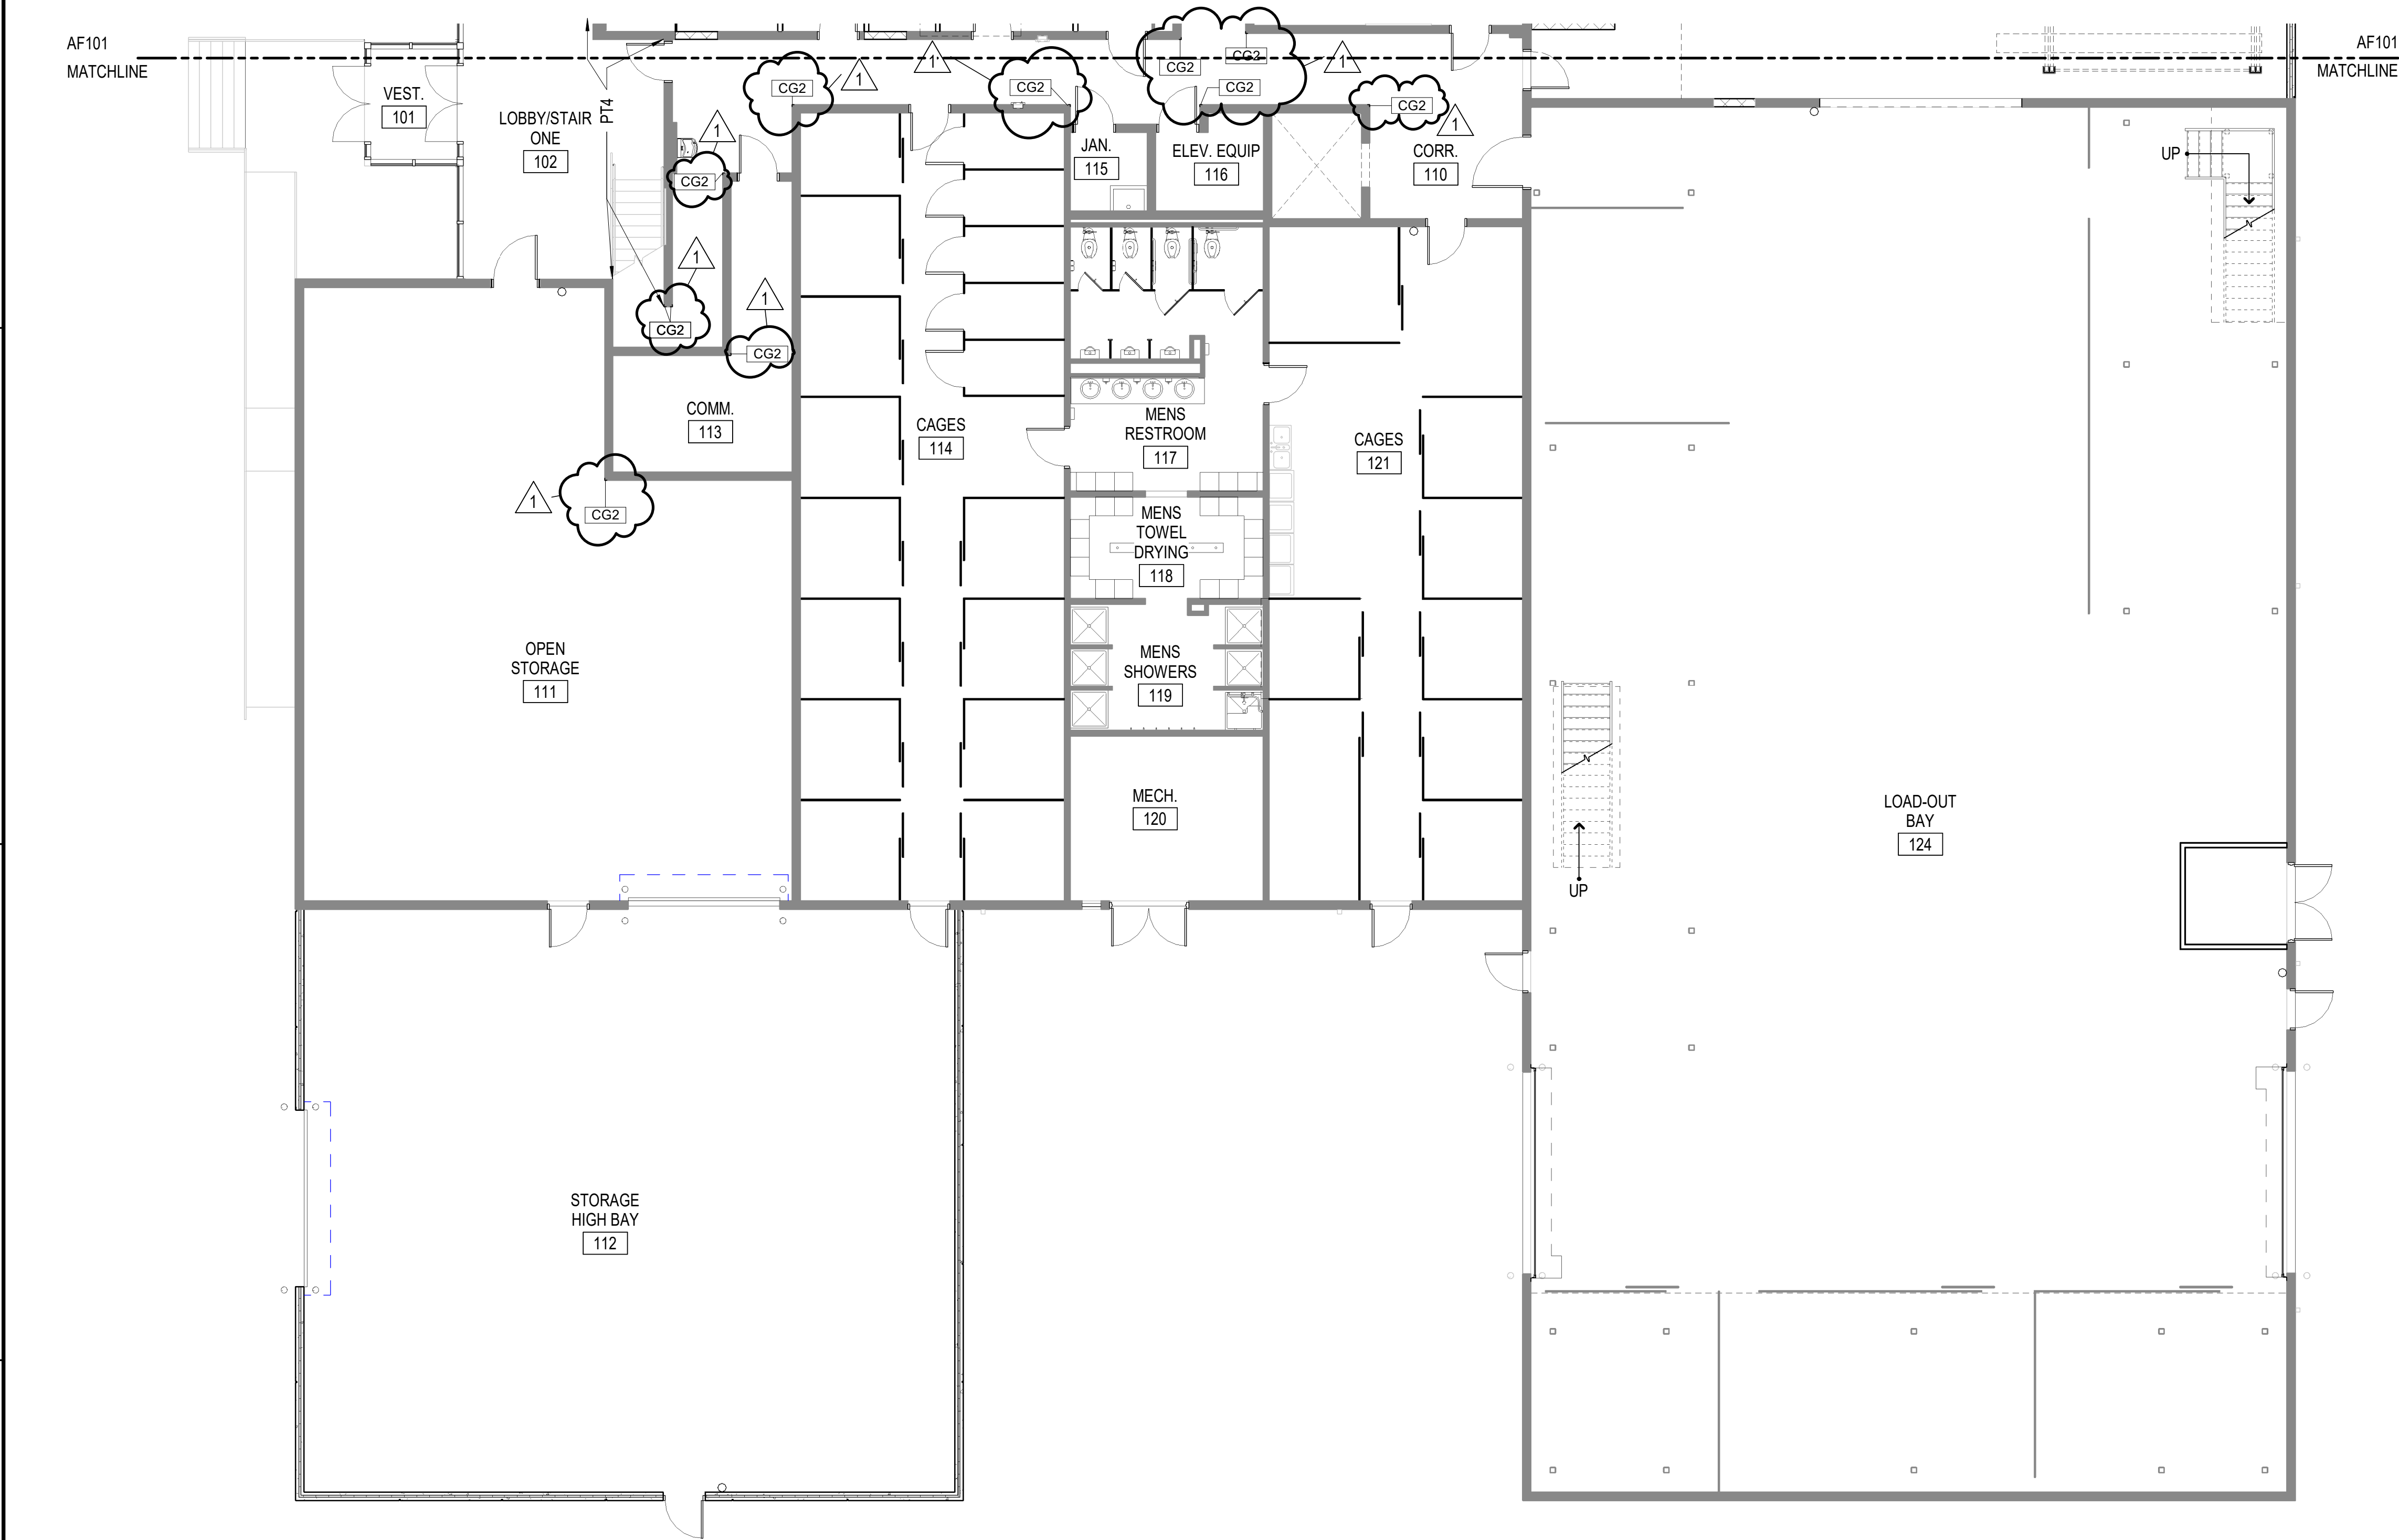

FIRST FLOOR FINISH & SIGNAGE PLAN AREA B

1/8" = 1'-0"


GENERAL NOTES

1. REFER TO SHEET AG601 FOR SIGNAGE TYPES.
2. REFER TO SHEET AF601 FOR FINISH SCHEDULE AND LEGEND.
3. REFER TO SPECIFICATION SECTION 10 14 00.20 INTERIOR SIGNAGE FOR INTERIOR SIGNAGE SCHEDULE.

SIGNAGE LEGEND

- ###
▼ SIGNAGE SYMBOL CODED TO AG601

KEY PLAN

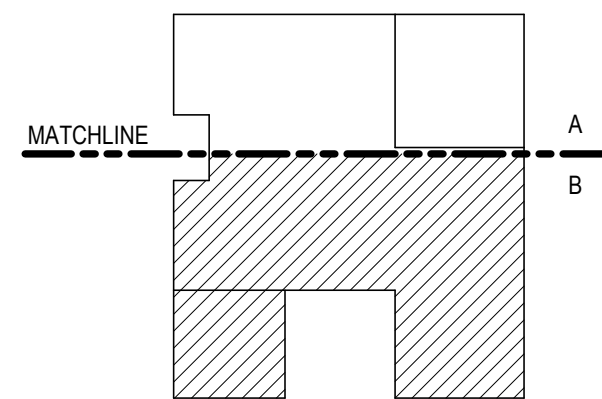

GRAPHIC SCALE(S)

1/8" = 1' - 0" 0 5' 10' 15' 30'

SYN	DESCRIPTION	DATE	APPR
1	CONSOLIDATED REVISIONS	11/21/25	



CLARK NEXSEN
A JMT Company
4525 MAIN STREET
SUITE 1400
VIRGINIA BEACH, VA 23462
757-455-5800 FAX 757-455-5638
WWW.CLARKNEXSEN.COM

APPROVED
FOR COMMANDER NAVFAC
ACTIVITY Approved by Don Bryant, PE, N10 Facilities Engineer, NSWDG via Email
SATISFACTORY TO DATE 07/09/2025
DES RMM DRW RMM CHK SBD
PMOM JT/SW
BRANCH MANAGER DJD
CHIEF ENGINEER JWW
FIRE PROTECTION HPN

DEPARTMENT OF THE NAVY
NAVAL FACILITIES ENGINEERING SYSTEMS COMMAND
NAVAL FACILITIES ENGINEERING SYSTEMS COMMAND - MID-ATLANTIC
NAVAL STATION - NORFOLK, VA
NAS OCEANA, DAM NECK ANNEX
Q-1075 SOF OPERATIONS BUILDING ADDITION
VIRGINIA BEACH, VA
FIRST FLOOR FINISH & SIGNAGE PLAN AREA B

SCALE: AS NOTED
PROJECT NO.: 1625040
CONSTR. CONTR. NO. N40085-19-D-9041
NAVFAC DRAWING NO. 12929007
SHEET 102 OF 239
AF102

DRAWING REVISION: 25 AUGUST 2020

GENERAL NOTES

- 1. REFER TO SHEET AG601 FOR SIGNAGE TYPES.
- 2. REFER TO SHEET AF601 FOR FINISH SCHEDULE AND LEGEND.
- 3. REFER TO SPECIFICATION SECTION 10 14 00.20 INTERIOR SIGNAGE FOR INTERIOR SIGNAGE SCHEDULE.


KEY NOTES

- 3. PROVIDE 60"W X 48"H GLASS, MAGNETIC WHITEBOARD AND ALUMINUM MARKER TRAY MOUNTED 44" AFF TO BOTTOM OF BOARD.
- 4. PROVIDE 96"W X 48"H GLASS, MAGNETIC WHITEBOARD WITH WORLD MAP AND ALUMINUM MARKER TRAY MOUNTED 2" ABOVE SEAT BACK TO BOTTOM OF BOARD.
- 5. PROVIDE 96"W X 48"H GLASS, MAGNETIC WHITEBOARD AND ALUMINUM MARKER TRAY MOUNTED 44" AFF TO BOTTOM OF BOARD.
- 6. PROVIDE 36"W X 48"H GLASS, MAGNETIC WHITEBOARD AND ALUMINUM MARKER TRAY MOUNTED 44" AFF TO BOTTOM OF BOARD.
- 7. REFER TO DETAIL D3 ON SHEET AE802 FOR UPHOLSTERED AUDIENCE SEAT
- 10. PROVIDE 60"W X 48"H GLASS, MAGNETIC WHITEBOARD AND ALUMINUM MARKER TRAY MOUNTED 2" ABOVE SEAT BACK TO BOTTOM OF WHITEBOARD.
- 11. PROVIDE 96"W X 48"H GLASS, MAGNETIC WHITEBOARD AND ALUMINUM MARKER TRAY MOUNTED 2" ABOVE SEAT BACK TO BOTTOM OF WHITEBOARD.



SIGNAGE LEGEND

- ### SIGNAGE SYMBOL CODED TO AG601


KEY PLAN

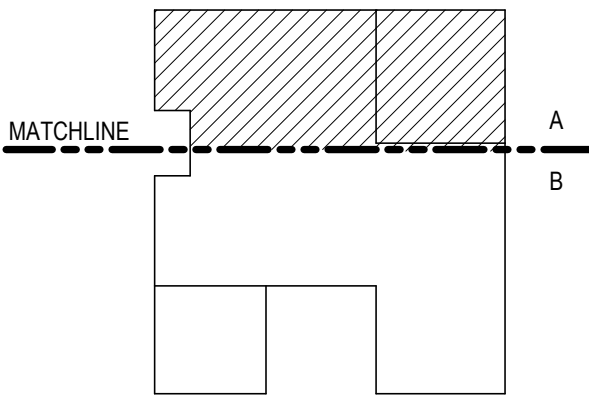


GRAPHIC SCALE(S)

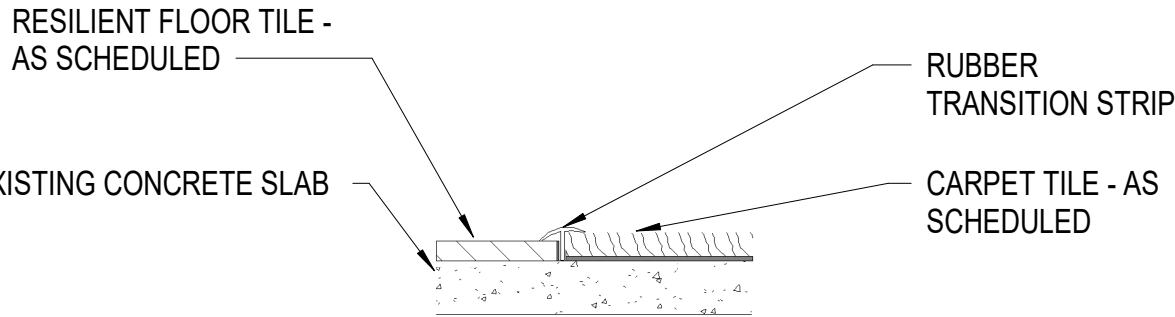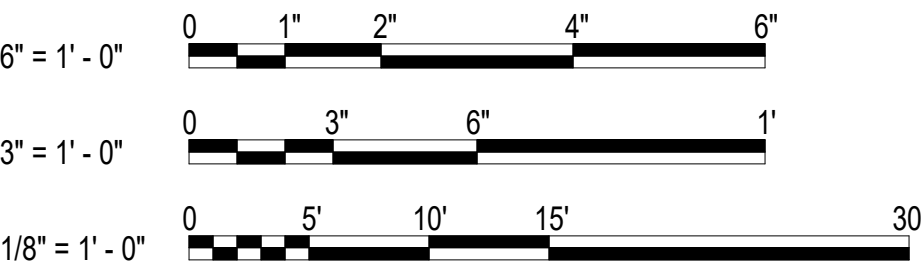


D3 RESILIENT FLOOR TILE TO CARPET TILE TRANSITION
6" = 1'-0"

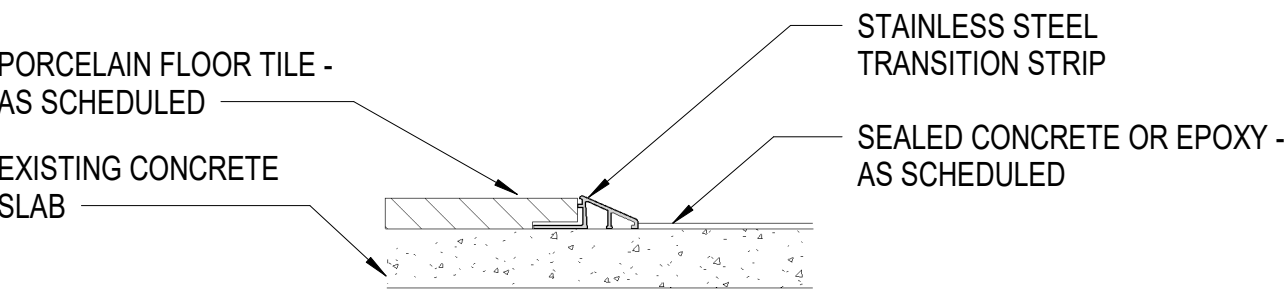

C1 PORCELAIN FLOOR TILE TO CONCRETE FLOOR TRANSITION
6" = 1'-0"

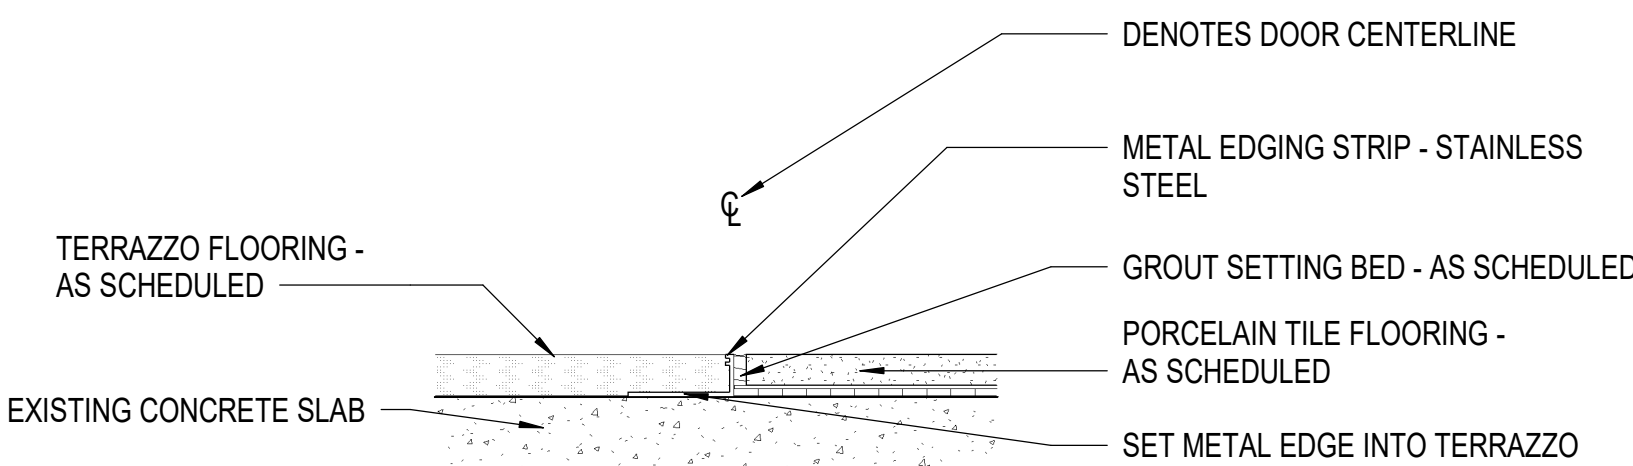

C3 TERRAZZO TO PORCELAIN TILE TRANSITION
3" = 1'-0"

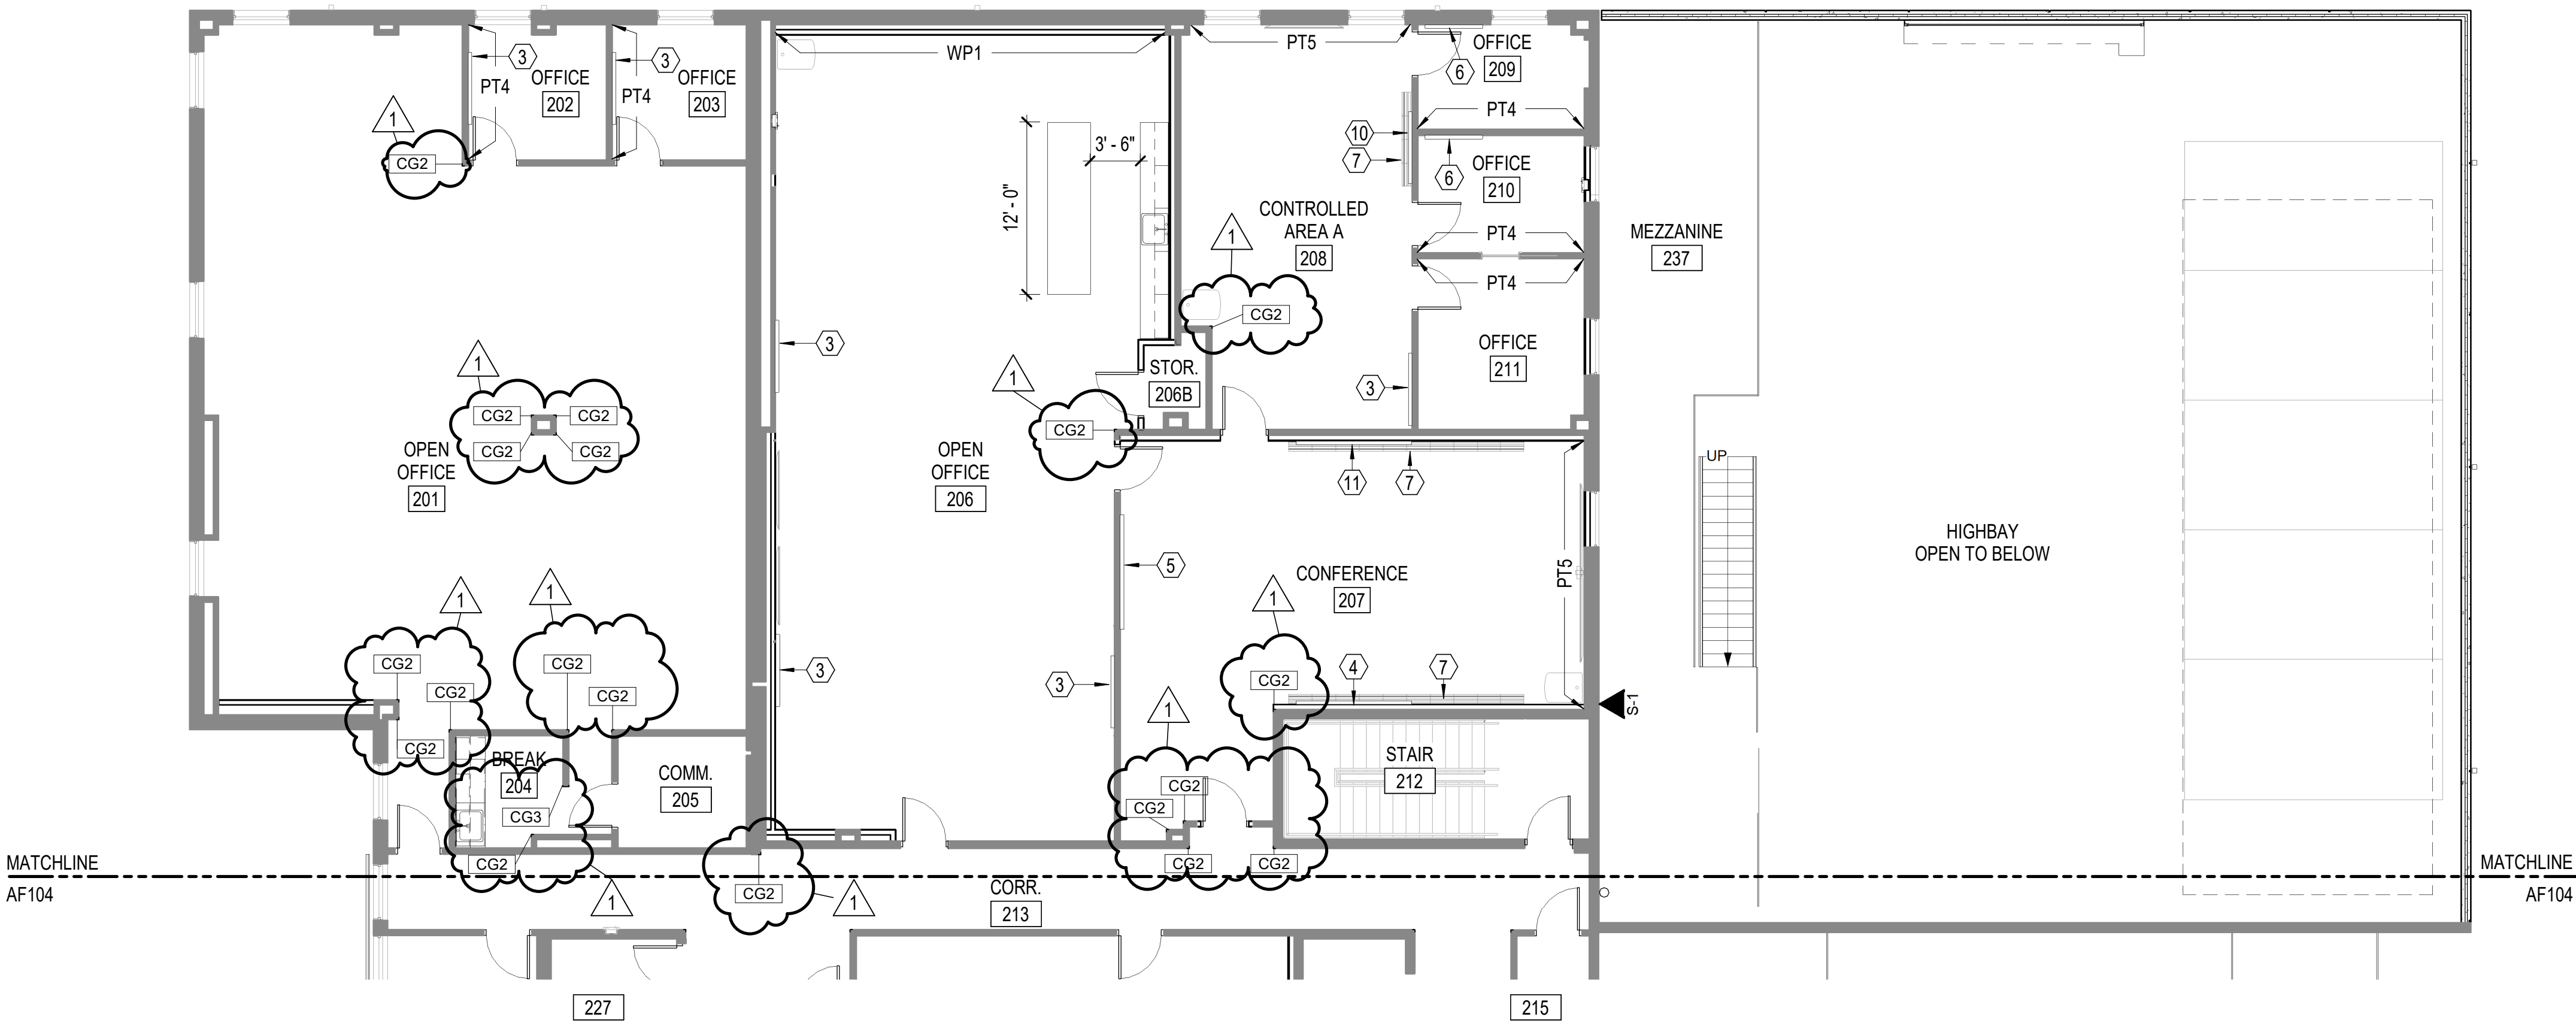

A1 SECOND FLOOR FINISH & SIGNAGE PLAN AREA A
1/8" = 1'-0"

DATE	SYMBOL	DESCRIPTION	APPROVED
11/02/25	1	CONSOLIDATED REVISIONS	



CLARK NEXSEN
A JAMT Company
4525 MAIN STREET
SUITE 1400
VIRGINIA BEACH, VA 23462
757-455-5800 FAX 757-455-5638
WWW.CLARKNEXSEN.COM


APPROVED	AW INFO
FOR COMMANDER NAVFAC	
ACTIVITY	Approved by Don Bryant, PE, N10 Facilities Engineer, NSWDG via Email
SATISFACTORY TO DATE	07/09/2025
DES	RMM
DRW	RMM
CHK	SBD
PMOM	JT/SW
BRANCH MANAGER	DJD
CHIEF ENGINEER	JWJ
FIRE PROTECTION	HPN

DEPARTMENT OF THE NAVY
NAVAL FACILITIES ENGINEERING SYSTEMS COMMAND
NAVAL FACILITIES ENGINEERING SYSTEMS COMMAND - MID-ATLANTIC
NAVAL STATION - NORFOLK, VA
NAS OCEANA, DAM NECK ANNEX
Q-1075 SOF OPERATIONS BUILDING ADDITION
VIRGINIA BEACH, VA
SECOND FLOOR FINISH & SIGNAGE PLAN AREA A

SCALE: AS NOTED
PROJECT NO.: 1625040
CONSTR. CONTR. NO. N40085-19-D-9041
NAVFAC DRAWING NO. 12929008
SHEET 103 OF 239
AF103

DRAWING REVISION: 25 AUGUST 2020

11/19/2025 1:58:03 AM AF 104
C:\Revit\Projects\BLDG\075-1625040-A_Relaym_Maler.rvt

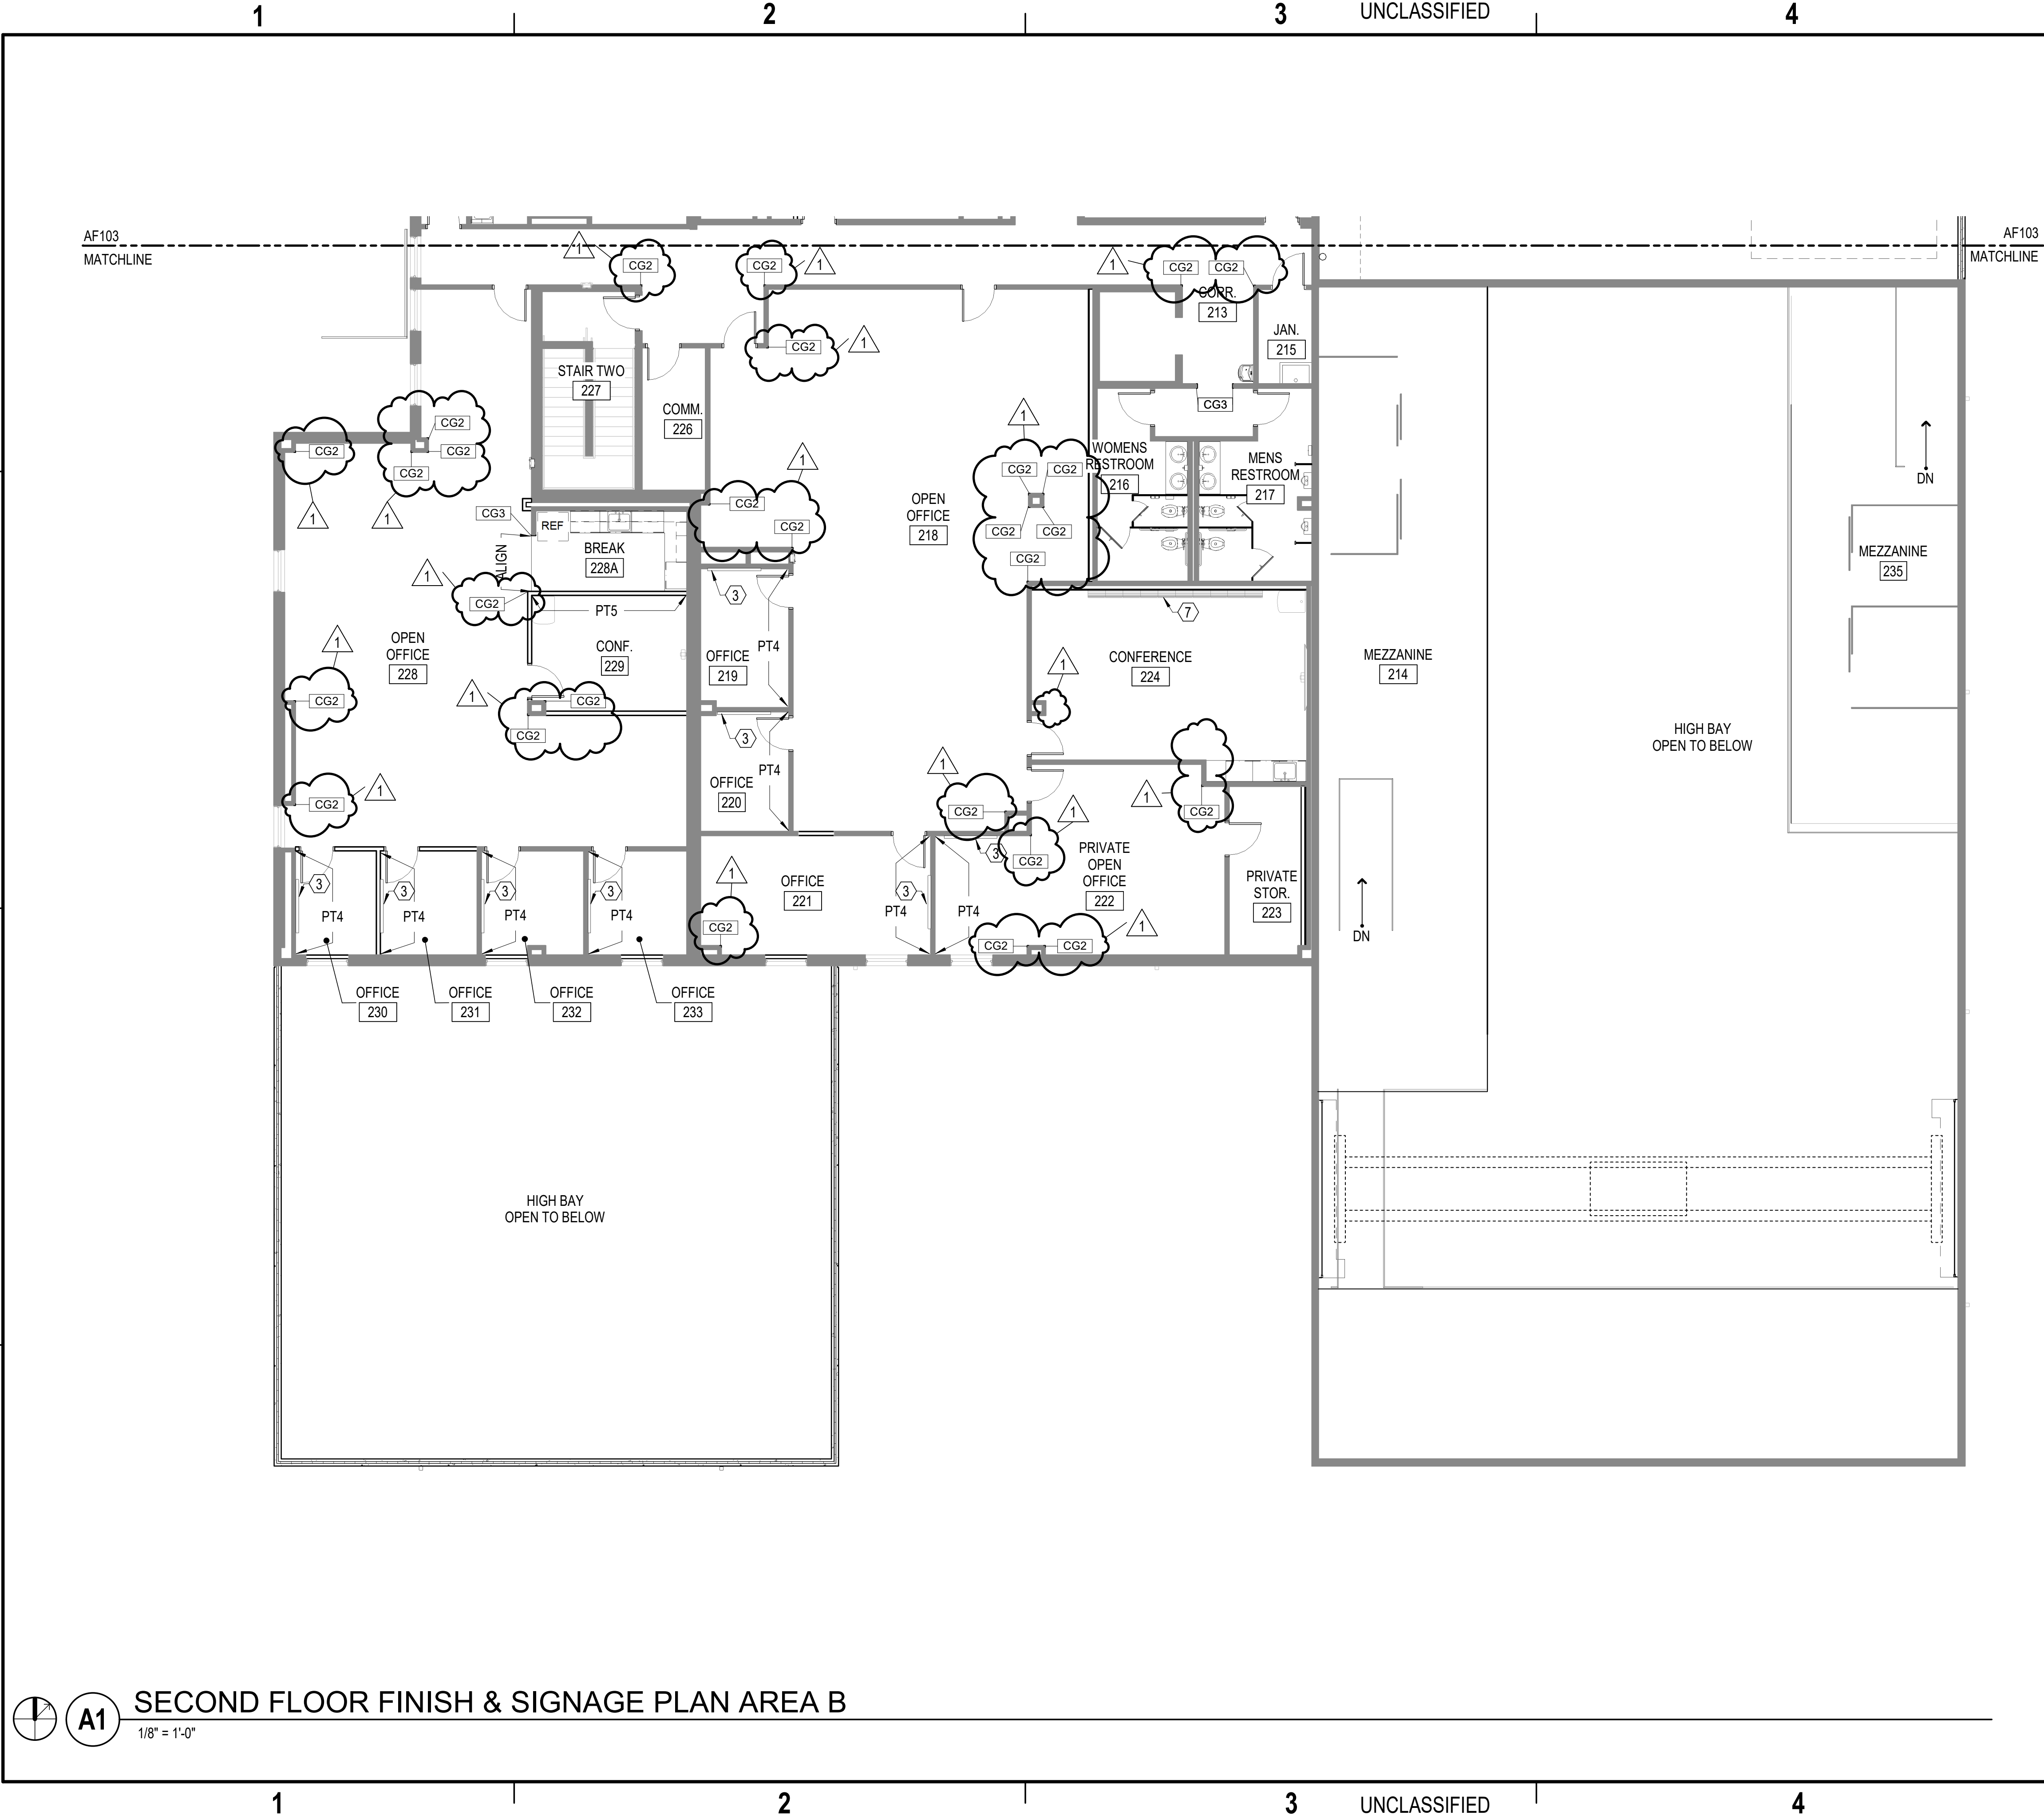

GENERAL NOTES

- REFER TO SHEET AG601 FOR SIGNAGE TYPES.
- REFER TO SHEET AF601 FOR FINISH SCHEDULE AND LEGEND.
- REFER TO SPECIFICATION SECTION 10 14 00.20 INTERIOR SIGNAGE FOR INTERIOR SIGNAGE SCHEDULE.

KEY NOTES

- PROVIDE 60"W X 48"H GLASS, MAGNETIC WHITEBOARD AND ALUMINUM MARKER TRAY MOUNTED 44" AFF TO BOTTOM OF BOARD.
- REFER TO DETAIL D3 ON SHEET AE802 FOR UPHOLSTERED AUDIENCE SEAT

SIGNAGE LEGEND

▼ SIGNAGE SYMBOL CODED TO AG601

KEY PLAN

GRAPHIC SCALE(S)

1/8" = 1'-0"

11/19/2025	11/2/25	DATE	APPR
1	CONSOLIDATED REVISIONS	SYM	DESCRIPTION

CLARKNEXSEN
A JMT Company
4525 MAIN STREET SUITE 1400
VIRGINIA BEACH, VA 23462
757-455-5800 FAX 757-455-5638
WWW.CLARKNEXSEN.COM

APPROVED

FOR COMMANDER NAVFAC

ACTIVITY
Approved by Don Bryant, PE, N10
Facilities Engineer, NSWDG
via Email

SATISFACTORY TO DATE 07/09/2025

DES	RMM	BRW	RMM	CHK	SBD
-----	-----	-----	-----	-----	-----

PMOM JT/SW

BRANCH MANAGER DJD

CHIEF ENGINEER JWL

FIRE PROTECTION HPN

DEPARTMENT OF THE NAVY
NAVAL FACILITIES ENGINEERING SYSTEMS COMMAND
NAVAL FACILITIES ENGINEERING SYSTEMS COMMAND - MID-ATLANTIC
NAVAL STATION - NORFOLK, VA
NAS OCEANA, DAM NECK ANNEX
Q-1075 SOF OPERATIONS BUILDING ADDITION
SECOND FLOOR FINISH & SIGNAGE PLAN AREA B

SCALE: AS NOTED

PROJECT NO.: 1625040

CONSTR. CONTR. NO. N40085-19-D-9041

NAVFAC DRAWING NO. 12929009

SHEET 104 OF 239

AF104

DRAWING REVISION: 25 AUGUST 2020

1								2								3								4								5							
FINISH SCHEDULE - OPERATIONS BUILDING								FINISH LEGEND - OPERATIONS BUILDING								GENERAL NOTES								GENERAL NOTES								GENERAL NOTES							
ROOM FLOOR BASE WALLS CEILING								CODE MATERIAL DESCRIPTION								A. FINISHES INDICATED ARE THE APPROVED BASIS OF DESIGN TO CONVEY COLOR, PATTERN, TEXTURE, AND SALIENT CHARACTERISTICS ONLY. THE LISTING OF MANUFACTURER INFORMATION IS NOT INTENDED TO LIMIT THE SELECTION OF PRODUCTS PROVIDED BY OTHER MANUFACTURERS. PRODUCT SUBSTITUTIONS MEETING THE SPECIFIED CRITERIA WILL BE CONSIDERED AND MUST BE REVIEWED AND APPROVED BY THE INTERIOR DESIGNER OF RECORD (IDOR) AND THE CONTRACTING OFFICER.								B. INSTALL FINISHES PER MANUFACTURER'S WRITTEN GUIDELINES AND UTILIZING MANUFACTURER'S RECOMMENDED PRODUCTS AND ACCESSORIES.								C. PROVIDE DUAL ROLLER WINDOW SHADES, DRWS1, AT ALL EXTERIOR WINDOWS.							
NO. NAME CODE CODE CODE MATERIAL CODE REMARKS								ACT1 ACOUSTICAL CEILING TILE ARMSTRONG; STYLE: ULTIMA HIGH NRC #1942; COLOR: "WHITE"; SIZE: 24" x 24" x 7/8"; GRID: 9/16" BEVELED TEGULAR								D. WHERE LARGE FORMAT TILE IS PROVIDED (ANY EDGE EXCEEDING 15"), SUBSURFACE VARIANCE MUST NOT EXCEED 1/8" IN 10'-0", INCLUDING NO MORE THAN 1/16" IN 24" WHEN MEASURED FROM THE HIGH POINTS IN THE SURFACE. PROVIDE FLOOR LEVELING ACCOMMODATION TO MEET THIS REQUIREMENT.								E. PAINT VERTICAL FACE AND UNDERSIDE OF CEILING SOFFITS, PT2, U.O.N.								F. PAINT INTERIOR DOORS AND FRAMES, PT3. PAINT METAL STAIR COMPONENTS, PT3.							
FIRST FLOOR								CG1 CORNER GUARD CS GROUP; STYLE: CO SERIES; MODEL #CO-8; COLOR: STAINLESS STEEL; WING SIZE: 3-1/2"; HEIGHT: 8'-0"								G. PAINT COLUMNS, PT3, U.O.N.								H. PROVIDE TOILET PARTITIONS, TP1, SEE ARCHITECTURAL SHEETS FOR ADDITIONAL INFORMATION.								I. PROVIDE GROUT WITH THE FOLLOWING PORCELAIN TILES:							
101 VEST. TZ1 --- --- --- ---								CG2 STAINLESS STEEL CORNER GUARD CS GROUP; STYLE: CO SERIES; MODEL #SCO-8; COLOR: STAINLESS STEEL; WING SIZE: 3-1/2"; HEIGHT: 8'-0"								J. WHERE FLOORING MATERIALS CHANGE, PROVIDE MANUFACTURER'S RECOMMENDED METAL TRANSITION STRIP WHEN MATERIAL HEIGHTS DIFFER. PROVIDE MANUFACTURER'S RECOMMENDED METAL EDGE PROTECTION WHEN MATERIAL HEIGHTS ARE THE SAME.								K. PROVIDE SOLID SURFACE SHOWER PANS AND SHOWER WALL PANEL SYSTEMS IN MANUFACTURERS STANDARD "WHITE".								L. PROVIDE METAL TILE EDGE PROTECTION AS SHOWN ON DETAIL AF101/D2.							
102 LOBBY/STAIR ONE PRC1/RST1 PRC6 PT1/PT4 ACOUSTICAL CEILING TILE ACT1 5								CG3 STAINLESS STEEL END WALL PROTECTOR CS GROUP; STYLE: CO SERIES; MODEL #SCO-8; COLOR: STAINLESS STEEL; WING SIZE: 3-1/2"; HEIGHT: 8'-0"								a. TILE WALL TO TILE WALL OUTSIDE CORNER BASIS OF DESIGN: SCHLUTER SCHIENE.								b. TILE WALL TO TILE WALL INSIDE CORNER BASIS OF DESIGN: SCHLUTER DILEX EHK.								c. TILE FLOOR TO TILE WALL INSIDE TRANSITION BASIS OF DESIGN: SCHLUTER DILEX EHK.							
103 MEN'S CAGES EP1 RB1 PT1 EXPOSED PT2								CG4 CORNER GUARD CS GROUP; STYLE: CO SERIES; MODEL #SCO-8; COLOR: STAINLESS STEEL; WING SIZE: 3-1/2"; HEIGHT: 8'-0"								d. EXCEPT IN 102 LOBBY/STAIR ONE, PROVIDE BULLNOSE BASE, PRC6, IN LIEU OF METAL COVE TRANSITION								M. LOCKER BENCH TO BE HIGH DENSITY POLYETHYLENE (HDPE) TOP AND ALUMINUM PEDESTALS.								N. ELEVATOR FINISHES WILL BE EXISTING TO REMAIN.							
104 DEV 1 STORAGE EP1 RB1 PT1 EXPOSED PT2								CPT1 CARPET TILE PATCHRAFT; COLLECTION: INFRASTRUCTURE; SERIES: SCAFFOLD 10519; COLOR: BRACKET #00450 WITH ACCENT THREAD #5484D; SIZE: 24" x 24"; SECONDARY BACKING: CUSHION BACKING; INSTALLATION: ASHLAR																															
105 WOMENS CAGES PRC1/EP1 RB1/--- PRC3/PRC4/PT1 MOISTURE RESISTANT GYPSUM BOARD/EXPOSED PT2 2								DRWS1 DUAL ROLLER WINDOW SHADES MECHOSHADE; MANUAL DUAL ROLLER SHADES; FABRIC COLLECTION: EUROTWILL; SERIES: 6000; COLOR: #8010 NICKEL, FABRIC #2 COLLECTION: CLASSIC BLACKOUT; SERIES: 0700; COLOR: #0711 "DARK GRAY"																															
106 WELLNESS ROOM RFT1 RB1 PT1 ACOUSTICAL CEILING TILE ACT1 1								EP1 EPOXY COATING SHERWIN WILLIAMS; SHERWIN WILLIAMS PRO INDUSTRIAL HIGH PERFORMANCE EPOXY; COLOR: #SW9143 "CADET"																															
107 BREACHERS STORAGE EP1 RB1 PT1 EXPOSED PT2								GR1 GROUT MAPEI; COLOR: #02 "PEWTER"																															
108 ELEC. SC1 RB1 PT1 EXPOSED PT2								GR2 GROUT MAPEI; COLOR: #09 "GRAY"																															
109 STAIR RST1/RFT2 RB1 PT1 --- --- 5								LK1 LOCKERS AND LOCKER ROOM BENCHES SCRANTON; COLLECTION: TUFFTEC LOCKERS; FINISH: ORANGE PEEL; COLOR: "CHARCOAL GREY"																															
110 CORR. EP1 RB1 PT1 ACOUSTICAL CEILING TILE ACT1								PL1 PLASTIC LAMINATE WILSONART; COLOR: # 7850-60 "BEIGEWOOD"; FINISH: MATTE																															
110B WOMENS SHOWERS PRC1 --- PRC3/PRC4 MOISTURE RESISTANT GYPSUM BOARD PT2								PL2 PLASTIC LAMINATE WILSONART; COLOR: D504K "FOSSIL SHALE"; FINISH: #18 LINEARITY FINISH																															
111 OPEN STORAGE EP1 RB1 PT1 EXPOSED PT2								PRC1 PORCELAIN TILE (FLOOR) CROSSVILLE; STYLE: TRAJECTORY; COLOR: #TRY03 "FLIGHT"; FINISH: UPS; SIZE: 12" x 24"; THICKNESS: 9.5MM; INSTALLATION: 33% OFFSET																															
112 STORAGE HIGH BAY EP1 RB1 PT1 EXPOSED PT2								PRC2 PORCELAIN TILE (FLOOR - MOSAIC) CROSSVILLE; STYLE: TRAJECTORY; COLOR: #TRY03 "FLIGHT"; FINISH: UPS; SIZE: 2" x 4"; THICKNESS: 9.5MM; INSTALLATION: ASHLAR																															
113 COMM. SC1 RB1 PT1 EXPOSED PT2								PRC3 PORCELAIN TILE (WALL) CROSSVILLE; STYLE: SHADES 2.0; COLOR: #SHD41 "FROST"; FINISH: SPO; SIZE: 12" x 24"; THICKNESS 9.5MM; INSTALLATION: 33% OFFSET																															
114 CAGES EP1 RB1 PT1 EXPOSED PT2								PRC4 PORCELAIN TILE (ACCENT) CROSSVILLE; STYLE: SHADES 2.0; COLOR: #SHD46 "ASH" FINISH: PTN; SIZE: 12" x 24"; THICKNESS: 9.5MM; INSTALLATION: 33% OFFSET																															
115 JAN. SC1 RB1 PT1 EXPOSED PT2 6								PRC5 PORCELAIN TILE NOT USED																															
116 ELEV. EQUIP SC1 RB1 PT1 EXPOSED PT2								PRC6 PORCELAIN TILE (BULLNOSE BASE) CROSSVILLE; STYLE: TRAJECTORY; COLOR: #TRY03 "FLIGHT"; FINISH: UPS; SIZE: 4" x 24"; THICKNESS: 9.5MM; INSTALLATION: ALIGN GROUT JOINTS WITH FLOOR TILE																															
117 MENS RESTROOM PRC2 --- PRC3/PRC4 MOISTURE RESISTANT GYPSUM BOARD PT2 2								PT1 PAINT (GENERAL) SHERWIN WILLIAMS; COLOR: #SW 6232 "MISTY"																															
118 MENS TOWEL DRYING PRC2 --- PRC3/PRC4 MOISTURE RESISTANT GYPSUM BOARD PT2 3								PT2 PAINT (CEILING) SHERWIN WILLIAMS; COLOR: #SW 7005 "PURE WHITE"																															
119 MENS SHOWERS PRC2 --- PRC3/PRC4 MOISTURE RESISTANT GYPSUM BOARD PT2								PT3 PAINT (TRIM) SHERWIN WILLIAMS; COLOR: #SW 7074 "SOFTWARE"																															
120 MECH. SC1 RB1 PT1 EXPOSED PT2								PT4 PAINT (ACCENT) SHERWIN WILLIAMS; COLOR: #SW 7608 "ADRIFT"																															
121 CAGES EP1 RB1 PT1 EXPOSED PT2								PT5 PAINT (ACCENT) SHERWIN WILLIAMS; COLOR: #SW 7619 "LABRADORITE"																															
122 CORRIDOR EP1 RB1 PT1 EXPOSED PT2								PT6 PAINT (TRIM ACCENT) SHERWIN WILLIAMS; COLOR: #SW 6234 "UNCERTAIN GRAY"																															
123 HIGH BAY STORAGE EP1 RB1 PT1 EXPOSED PT2																																							