

1

2

3


UNCLASSIFIED

4

5

D


D

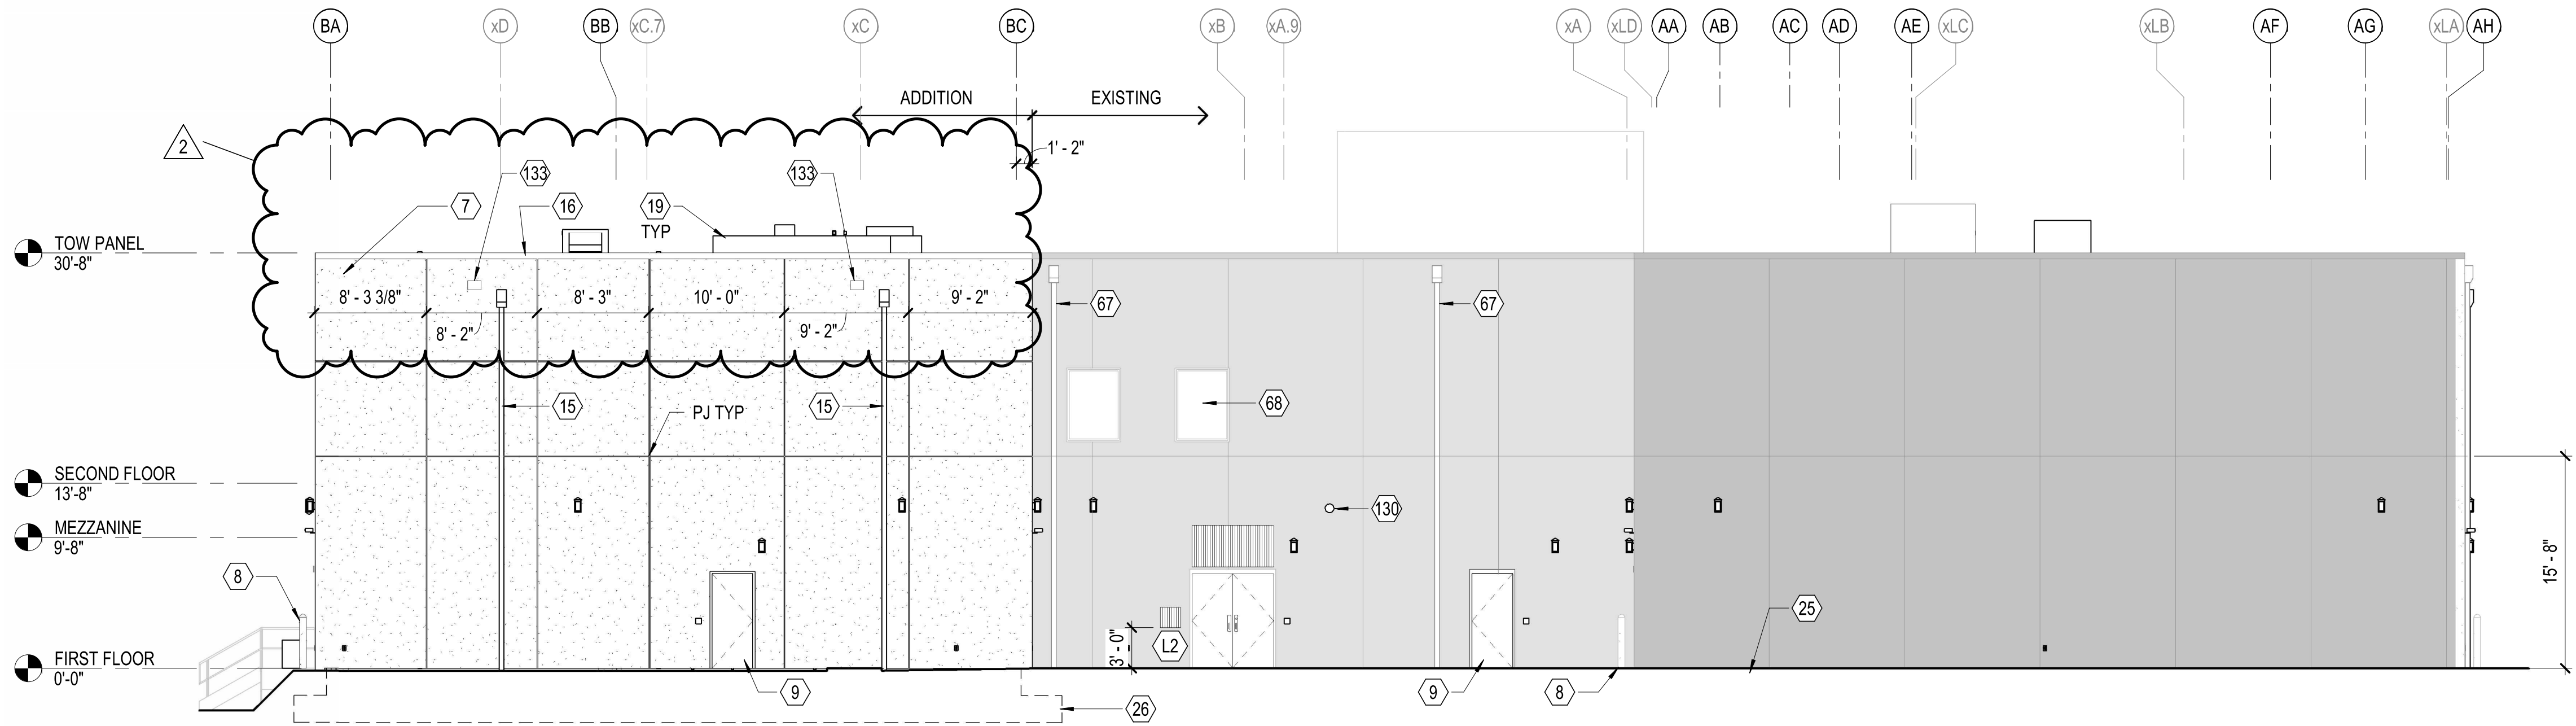

B4
AE101
C1 EXTERIOR BLDG ELEVATION - SOUTH
1/8" = 1'-0"

C

C

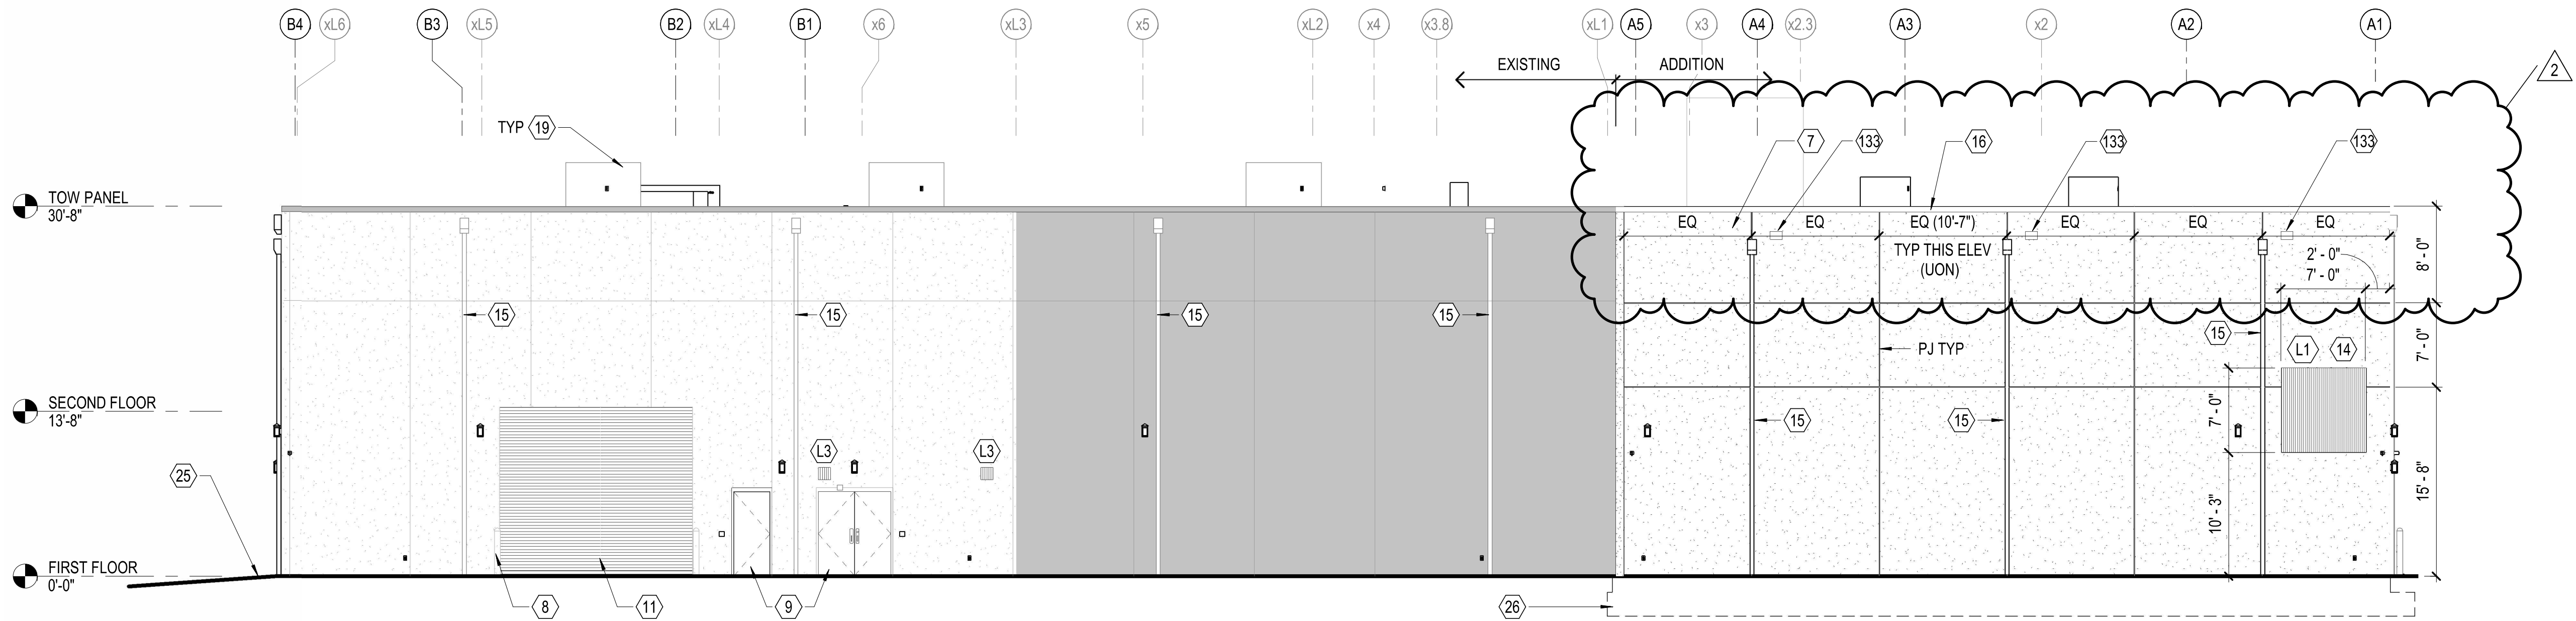

B4
AE101
A1 EXTERIOR BLDG ELEVATION - EAST
1/8" = 1'-0"

B

B

A

A

#	KEY NOTES	THIS SHEET ONLY
7	INSULATED PRECAST CONCRETE (PC-1) SANDWICH PANELS	
8	6" DIAMETER CONCRETE FILLED STEEL BOLLARD, COLOR TO BE "SAFETY YELLOW"	
9	PERSONNEL DOOR(S), REFER TO DOOR SCHEDULE ON AE601	
11	OVERHEAD COILING DOOR, SEE ADDITIONAL INFORMATION ON AE601	
14	PREFINISHED METAL STORM LOUVER, SEE ADDITIONAL INFORMATION ON SHEET AE703	
15	THRU WALL SCUPPER WITH PREFINISHED METAL CONDUCTOR HEAD & DOWNSPOUT (DS)- SEE DETAIL B4/AE503.	
16	PREFINISHED METAL PARAPET COPING (MTL-1)	
19	ROOFTOP MOUNTED MECHANICAL EQUIPMENT, COORDINATE WITH MECHANICAL DRAWINGS	
25	APPROXIMATE FINISH GRADE, COORDINATE WITH CIVIL DRAWINGS	
26	DASHED LINE INDICATES STRUCTURAL FOUNDATION, COORDINATE WITH STRUCTURAL DRAWINGS	

#	KEY NOTES	THIS SHEET ONLY
67	EXISTING DOWNSPOUT TO REMAIN	
68	EXISTING WINDOW TO REMAIN	
130	WATER HEATER INTAKE EXHAUST - SEE MECHANICAL	
133	THROUGH WALL OVERFLOW SCUPPER- SEE DETAIL D4/AE503.	

GENERAL NOTES	THIS SHEET ONLY
A. SEE SHEET AE201 FOR TYPICAL BUILDING ELEVATION GENERAL NOTES.	
GRAPHIC SCALE(S)	
1/8" = 1' - 0" 0 5' 10' 15' 30'	

12/8/2025 1:22:45 PM C:\Revit\Projects\BLDG-Q1075-1625040-A_msoe@clarknexsen.com.rvt	
AE202	
CLARKNEXSEN A JMT Company 4525 MAIN STREET SUITE 1400 VIRGINIA BEACH, VA 23462 757-455-5800 FAX 757-455-5638 WWW.CLARKNEXSEN.COM	
APPROVED	
FOR COMMANDER NAVFAC	
ACTIVITY Approved by Don Bryant, PE, N10 Facilities Engineer, NSWDG via Email	
SATISFACTORY TO DATE 07/09/2025	
DES DJH	DRW DJH
CHK RAM	PMOM JT/SW
BRANCH MANAGER DJD	CHIEF ENGINEER JWW
FIRE PROTECTION HPV	
NAVAL FACILITIES ENGINEERING SYSTEMS COMMAND NAVAL FACILITIES ENGINEERING SYSTEMS COMMAND - MID-ATLANTIC NAVAL STATION - NORFOLK, VA VIRGINIA BEACH, VA	
Q-1075 SOF OPERATIONS BUILDING ADDITION	
EXTERIOR ELEVATIONS	
SCALE: AS NOTED	
EPROJCT NO.: 1625040	
CONSTR. CONTR. NO. N40085-19-D-9041	
NAVFAC DRAWING NO. 12928988	
SHEET 83 OF 239	
AE202	
DRAWING REVISION: 25 AUGUST 2020	

1

2

3

UNCLASSIFIED

4

5