


12/8/2025 12:01:53 PM
C:\Revit\Projects\BLD\Q1075-162504-A_Thomas\pilot\B5\K5.vrt
G1011

A
B
C
D

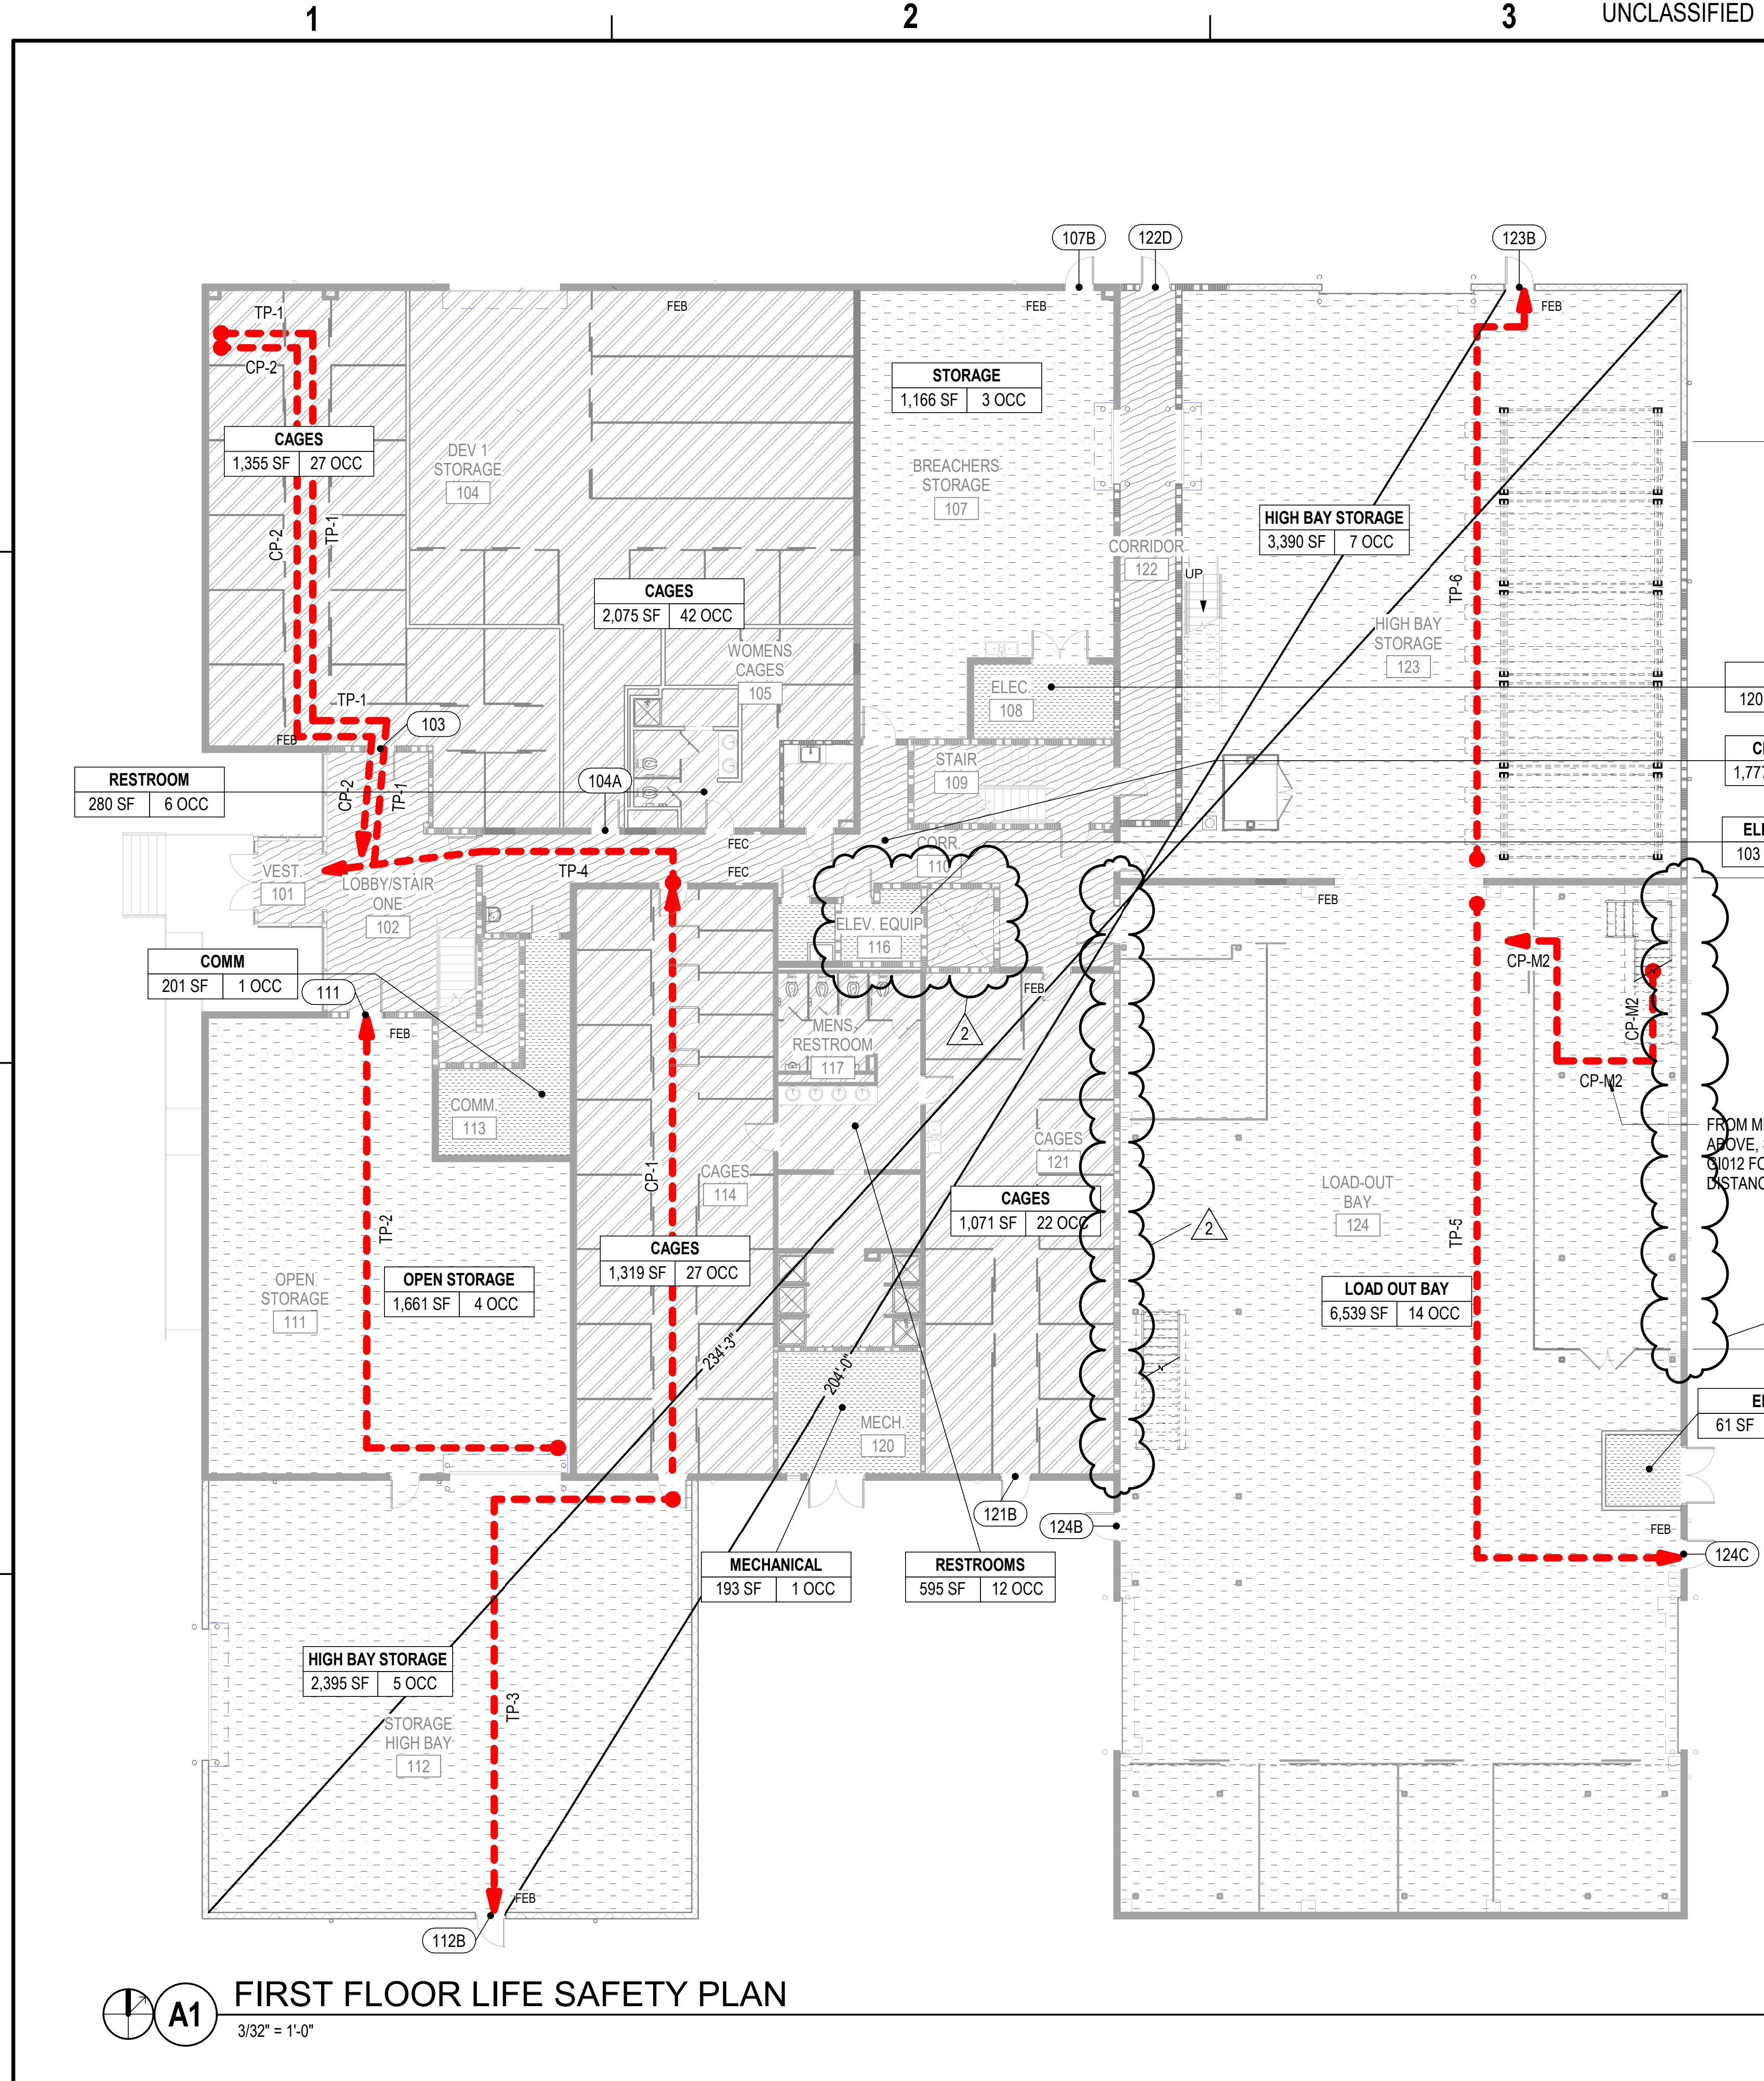


LIFE SAFETY - OCCUPANT CALCULATION - FIRST FLOOR						
LEVEL	PATTERN	OCCUPANCY	SF PER PERSON	OCCUPANCY SF TYPE	AREA	*NUMBER OF OCCUPANTS
FIRST FLOOR		BUSINESS AREAS	150	GROSS	1,777 SF	12
FIRST FLOOR		LOCKER ROOMS	50	GROSS	6,695 SF	136
FIRST FLOOR		MECHANICAL, ELECTRICAL, OTHER BUILDING EQUIPMENT	500	GROSS	678 SF	5
FIRST FLOOR		STORAGE	500	GROSS	15,151 SF	33
FIRST FLOOR TOTALS:					24,302 SF	186

* NUMBER OF OCCUPANTS IS AN AGGREGATE AND IS A RESULT OF ROUNDING UP INDIVIDUAL AREAS

PATH ID	DISTANCE
CP-1	62' - 0"
CP-2	57' - 6"
TP-1	74' - 6"
TP-2	66' - 6"
TP-3	63' - 0"
TP-4	102' - 6"
TP-5	91' - 6"
TP-6	65' - 6"

LIFE SAFETY - EGRESS DOOR SCHEDULE				
DOOR NO.	CLEAR EGRESS WIDTH PROVIDED	EGRESS WIDTH FACTOR	OCCUPANT LOAD	
			MAX PROVIDED	REQUIRED
FIRST FLOOR				
103	33"	0.2	165	27
104A	33"	0.2	165	42
107B	33"	0.2	165	3
111	39"	0.2	195	4
112B	33"	0.2	165	5
121B	33"	0.2	165	28
122D	33"	0.2	165	46
123B	33"	0.2	165	10
124B	33"	0.2	165	9
124C	33"	0.2	165	10

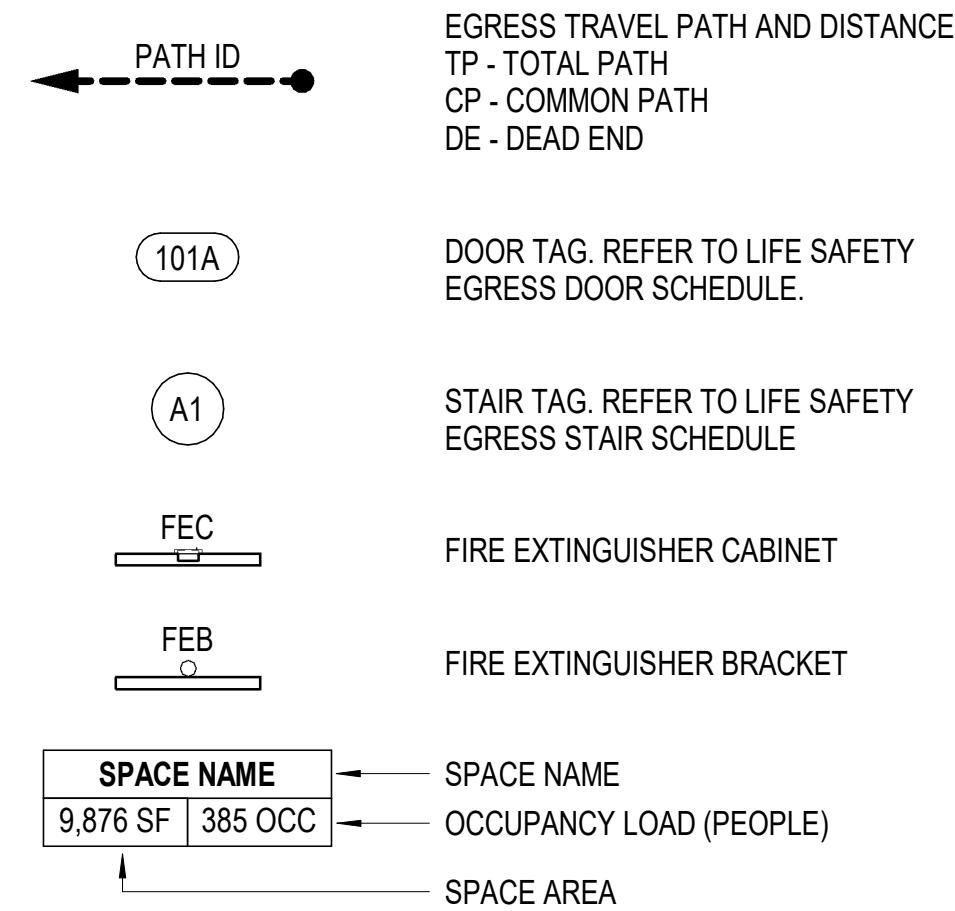

- COORDINATE ALL FIRE EXTINGUISHERS LOCATIONS SHOWN ON PLANS W/ LOCAL FIRE OFFICIAL'S REQUIREMENTS.
- GC TO PROVIDE & INSTALL ALL BLOCKING IN WALLS AS REQUIRED FOR MOUNTING FIRE EXTINGUISHERS.
- GC TO COORDINATE INSTALLATION REQUIREMENTS OF EXIT SIGNS, ALL ASSOCIATED HARDWARE, JUNCTION BOXES, WIRING & REQUIRED EXIT DEVICES W/ ELECTRICAL DRAWINGS & LOCAL INSPECTOR.
- RATED WALLS AND PARTITIONS REQUIRED TO HAVE PROTECTED OPENINGS SHALL BE PERMANENTLY STENCILED EVERY 10'-0" ABOVE THE CEILING OR CONCEALED SPACE.

EXAMPLE:
• 1-HOUR RATED BARRIER - PROTECT ALL OPENINGS

GRAPHIC SCALE(S)



A1 FIRST FLOOR LIFE SAFETY PLAN
3/32" = 1'-0"

12/8/25

DATE

APPR

2

CONSOLIDATED REVISIONS

SYM

DESCRIPTION

CLARKNEXSEN

A JMT Company

4525 MAIN STREET

SUITE 1400

VIRGINIA BEACH, VA 23462

757-455-5800 FAX 757-455-5638

WWW.CLARKNEXSEN.COM

APPROVED

FOR COMMANDER NAVFAC

ACTIVITY

Approved by Don Bryant, PE, N10

Facilities Engineer, NSWDG

via Email

SATISFACTORY TO DATE

07/09/2025

DES

EVA

DRW

EVA

CHK

CHB

PMOM

JT/SW

BRANCH MANAGER

HPN

CHIEF ENGINEER

JWJ

FIRE PROTECTION

HPN

DEPARTMENT OF THE NAVY

NAVAL FACILITIES ENGINEERING SYSTEMS COMMAND

NAVAL FACILITIES ENGINEERING SYSTEMS COMMAND - MID-ATLANTIC

NAVAL STATION - NORFOLK, VA

NAS OCEANA, DAM NECK ANNEX

Q-1075 SOF OPERATIONS BUILDING ADDITION

FIRST FLOOR LIFE SAFETY PLAN

SCALE: AS NOTED

EPROJCT NO.: 1625040

CONSTR. CONTR. NO. N40085-19-D-9041

NAVFAC DRAWING NO. 12928910

SHEET 5 OF 239

G1011

DRAWING REVISION: 25 AUGUST 2020

A
B
C
D

UNCLASSIFIED

D

C

B

A

D


C

UNCLASSIFIED

B


A

12/26/2025 12:01:55 PM
C:\Revit Projects\BLDG01075-1625040-A_Thomas\adent51\KS.vrt

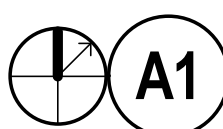

SECOND FLOOR LIFE SAFETY PLAN

3/32" = 1'-0"

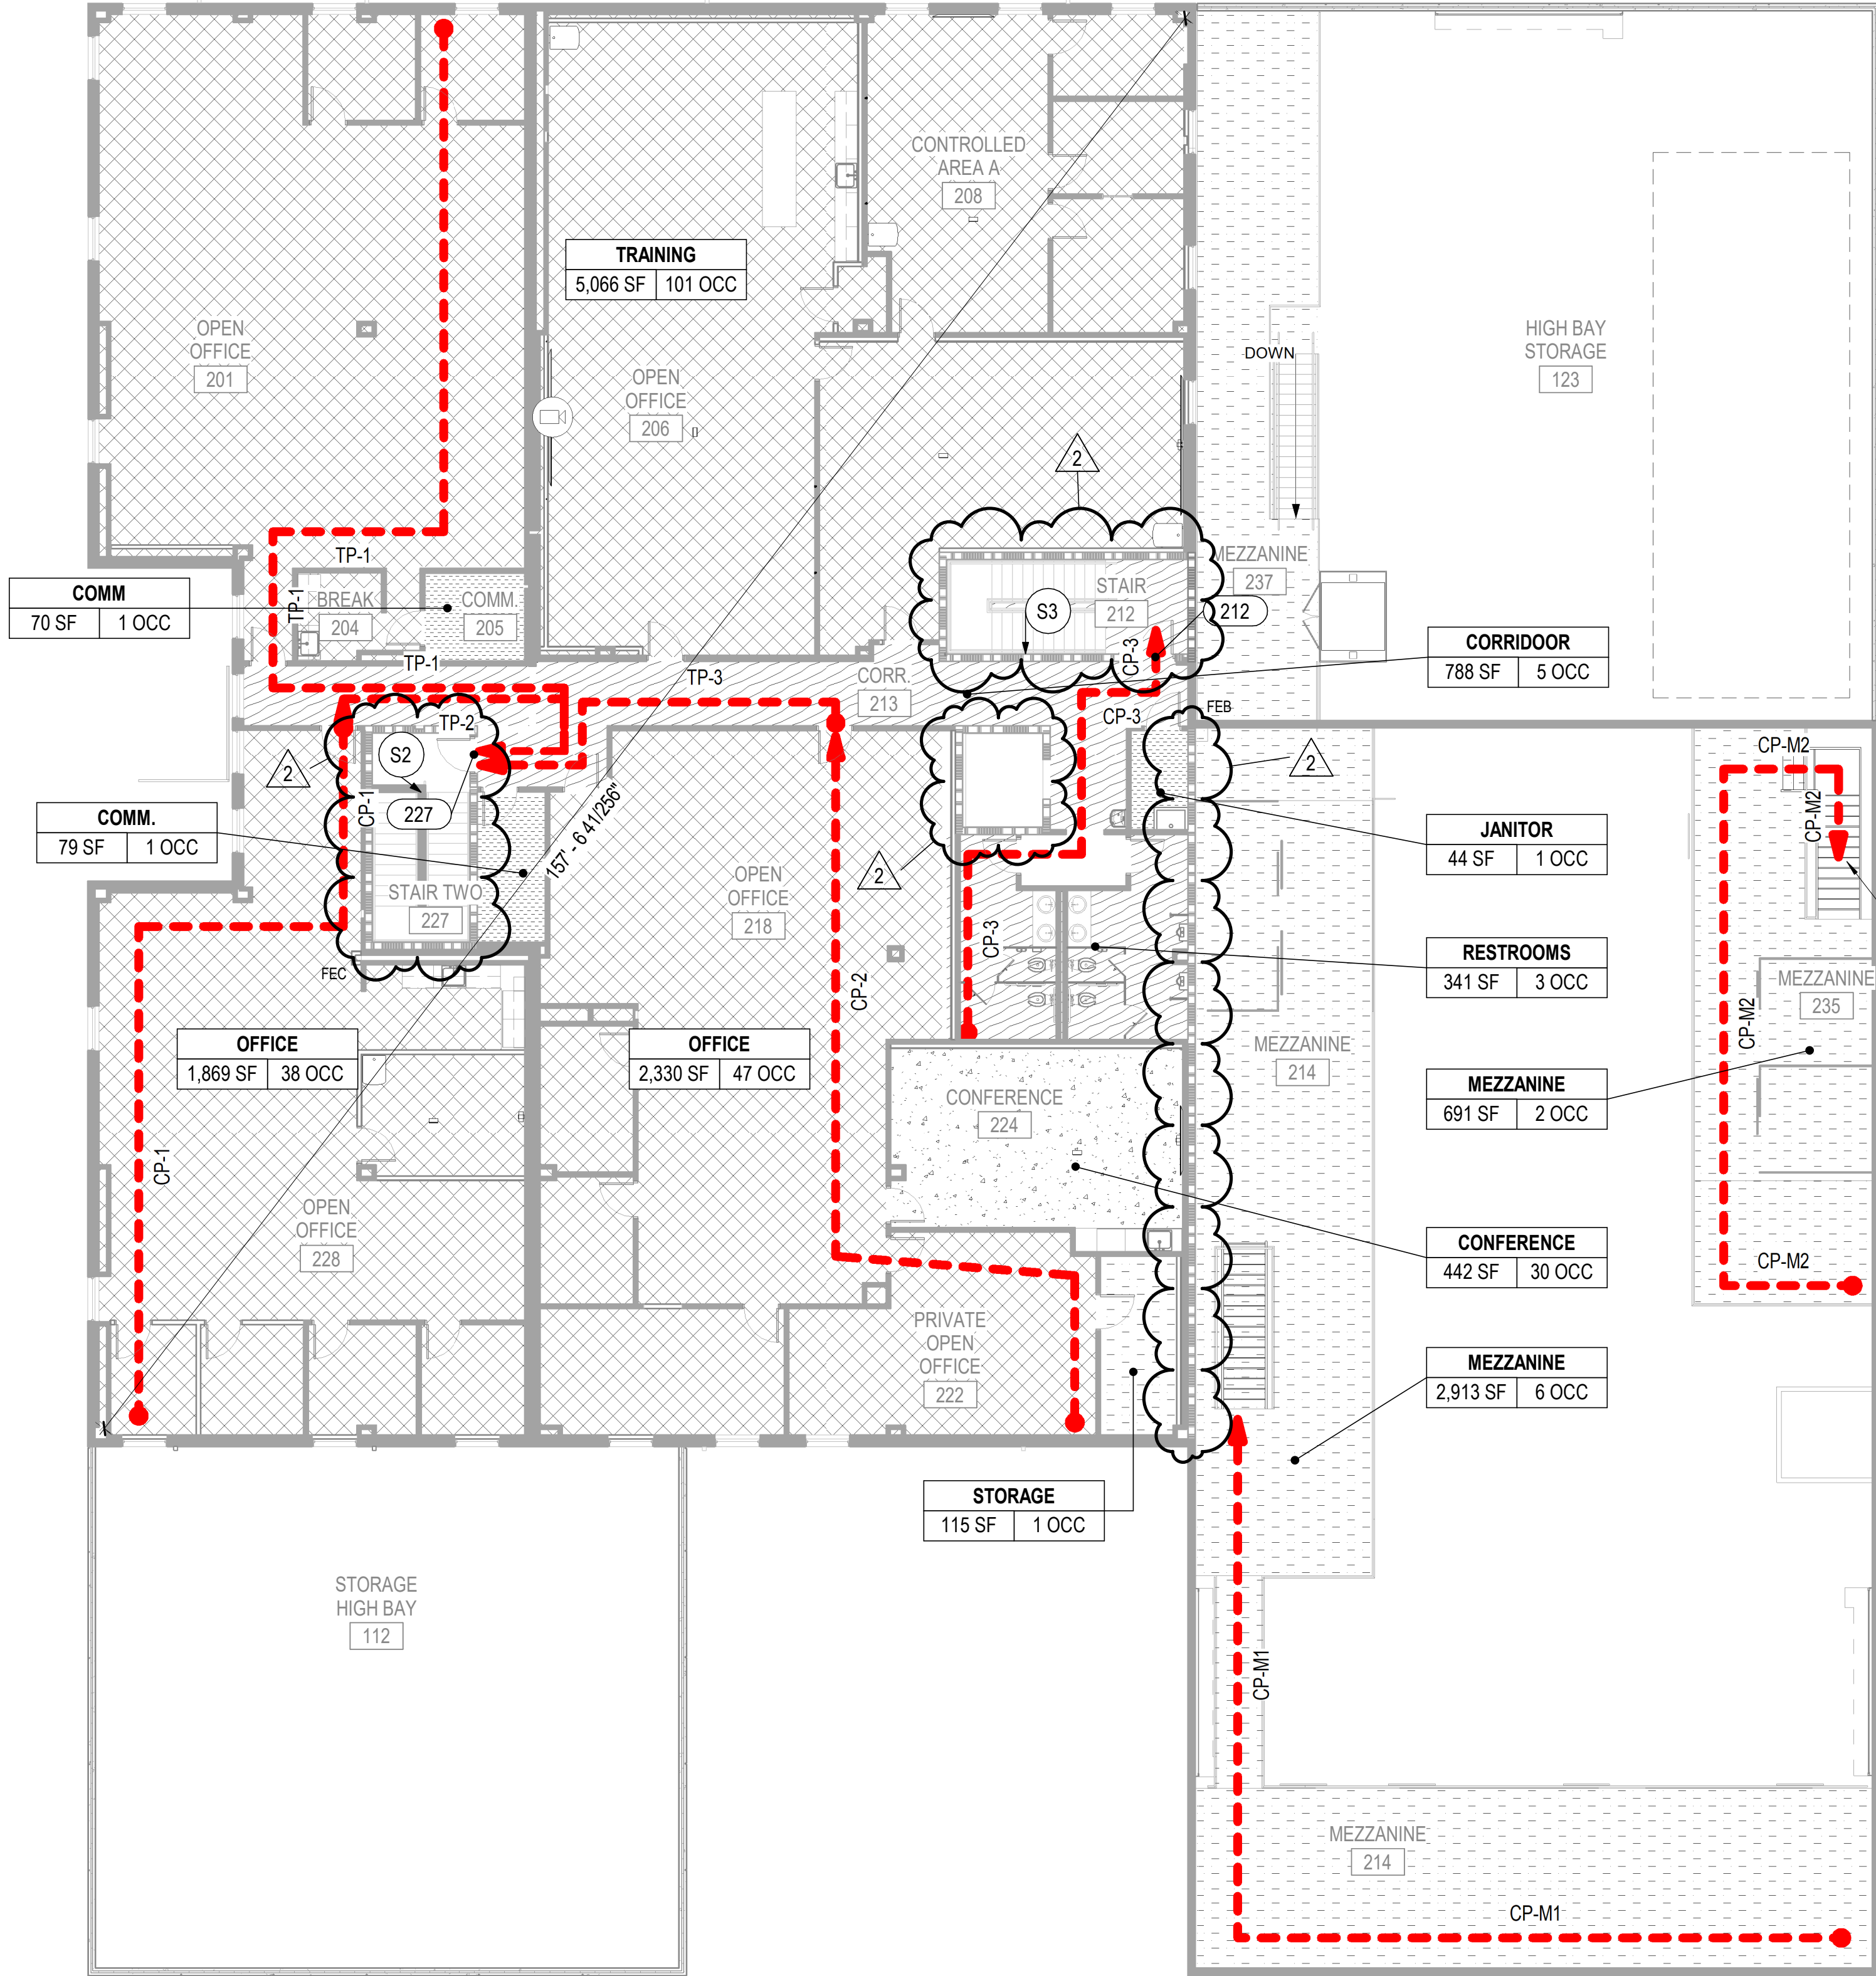

LIFE SAFETY - OCCUPANT CALCULATION - SECOND FLOOR						
LEVEL	PATTERN	OCCUPANCY	SF PER PERSON	OCCUPANCY SF TYPE	AREA	*NUMBER OF OCCUPANTS
SECOND FLOOR		ASSEMBLY LESS CONCENTRATED USE	15	NET	442 SF	30
SECOND FLOOR		BUSINESS AREAS	150	GROSS	1,130 SF	8
SECOND FLOOR		CONCENTRATED BUSINESS USE	50	GROSS	9,264 SF	186
SECOND FLOOR		MECHANICAL, ELECTRICAL, OTHER BUILDING EQUIPMENT	500	GROSS	192 SF	3
SECOND FLOOR		STORAGE	500	GROSS	3,719 SF	9
SECOND FLOOR TOTALS:					14,748 SF	236

* NUMBER OF OCCUPANTS IS AN AGGREGATE AND IS A RESULT OF ROUNDING UP INDIVIDUAL AREAS

PATH ID	DISTANCE
CP-1	81' - 6"
CP-2	80' - 6"
CP-3	52' - 6"
CP-M1	99' - 6"
CP-M2	113' - 0"
TP-1	112' - 6"
TP-2	116' - 0"
TP-3	119' - 6"

LIFE SAFETY - STAIR SCHEDULE					
TOP LEVEL	STAIR MARK	CLEAR STAIR WIDTH PROVIDED	EGRESS WIDTH FACTOR	MAX PROVIDED	OCCUPANT LOAD REQUIRED
SECOND FLOOR	S2	48"	0.3	160	75
SECOND FLOOR	S3	48"	0.3	160	76

LIFE SAFETY - EGRESS DOOR SCHEDULE				
DOOR NO.	CLEAR EGRESS WIDTH PROVIDED	EGRESS WIDTH FACTOR	OCCUPANT LOAD	
			MAX PROVIDED	REQUIRED
SECOND FLOOR				
212	33"	0.2	165	75
227	33"	0.2	165	76

PATH ID
EGRESS TRAVEL PATH AND DISTANCE
TP - TOTAL PATH
CP - COMMON PATH
DE - DEAD END

101A

DOOR TAG. REFER TO LIFE SAFETY EGRESS DOOR SCHEDULE.

A1

STAIR TAG. REFER TO LIFE SAFETY EGRESS STAIR SCHEDULE

FEC

FIRE EXTINGUISHER CABINET

FEB

FIRE EXTINGUISHER BRACKET

SPACE NAME	SPACE NAME
9,876 SF 385 OCC	OCCUPANCY LOAD (PEOPLE)
	SPACE AREA

- ONE HALF HOUR FIRE RATING
- ONE HOUR FIRE RATING
- TWO HOUR FIRE RATING
- THREE HOUR FIRE RATING
- FOUR HOUR FIRE RATING
- SMOKE BARRIER (SB), SMOKE PARTITION (SP), OR PARTITION CAPABLE OF RESISTING THE PASSAGE OF SMOKE (S)

GRAPHIC SCALE(S)



DATE	APPR
12/26/25	
SYM	DESCRIPTION
2	CONSOLIDATED REVISIONS



CLARKNEXSEN
A JMT Company
4525 MAIN STREET SUITE 1400
VIRGINIA BEACH, VA 23462
757-455-5800 FAX 757-455-5638
WWW.CLARKNEXSEN.COM

APPROVED	WE INFO
FOR COMMANDER NAVFAC	
ACTIVITY: Approved by Don Bryant, PE, N10 Facilities Engineer, NSWDG via Email	
SATISFACTORY TO DATE	07/09/2025
DES	EVA
DRW	EVA
CHK	CHB
PMCM	JT/SW
BRANCH MANAGER	HPN
CHIEF ENGINEER	JWJ
FIRE PROTECTION	HPN

DEPARTMENT OF THE NAVY
NAVAL FACILITIES ENGINEERING SYSTEMS COMMAND
NAVAL FACILITIES ENGINEERING SYSTEMS COMMAND - MID-ATLANTIC
NAVAL STATION - NORFOLK, VA
NAS OCEANA, DAM NECK ANNEX
Q-1075 SOF OPERATIONS BUILDING ADDITION
SECOND FLOOR LIFE SAFETY PLAN

SCALE: AS NOTED
PROJECT NO.: 1625040
CONSTR. CONTR. NO. N40085-19-D-9041
NAVFAC DRAWING NO. 12928911
SHEET 6 OF 239
G1012

DRAWING REVISION: 25 AUGUST 2020