



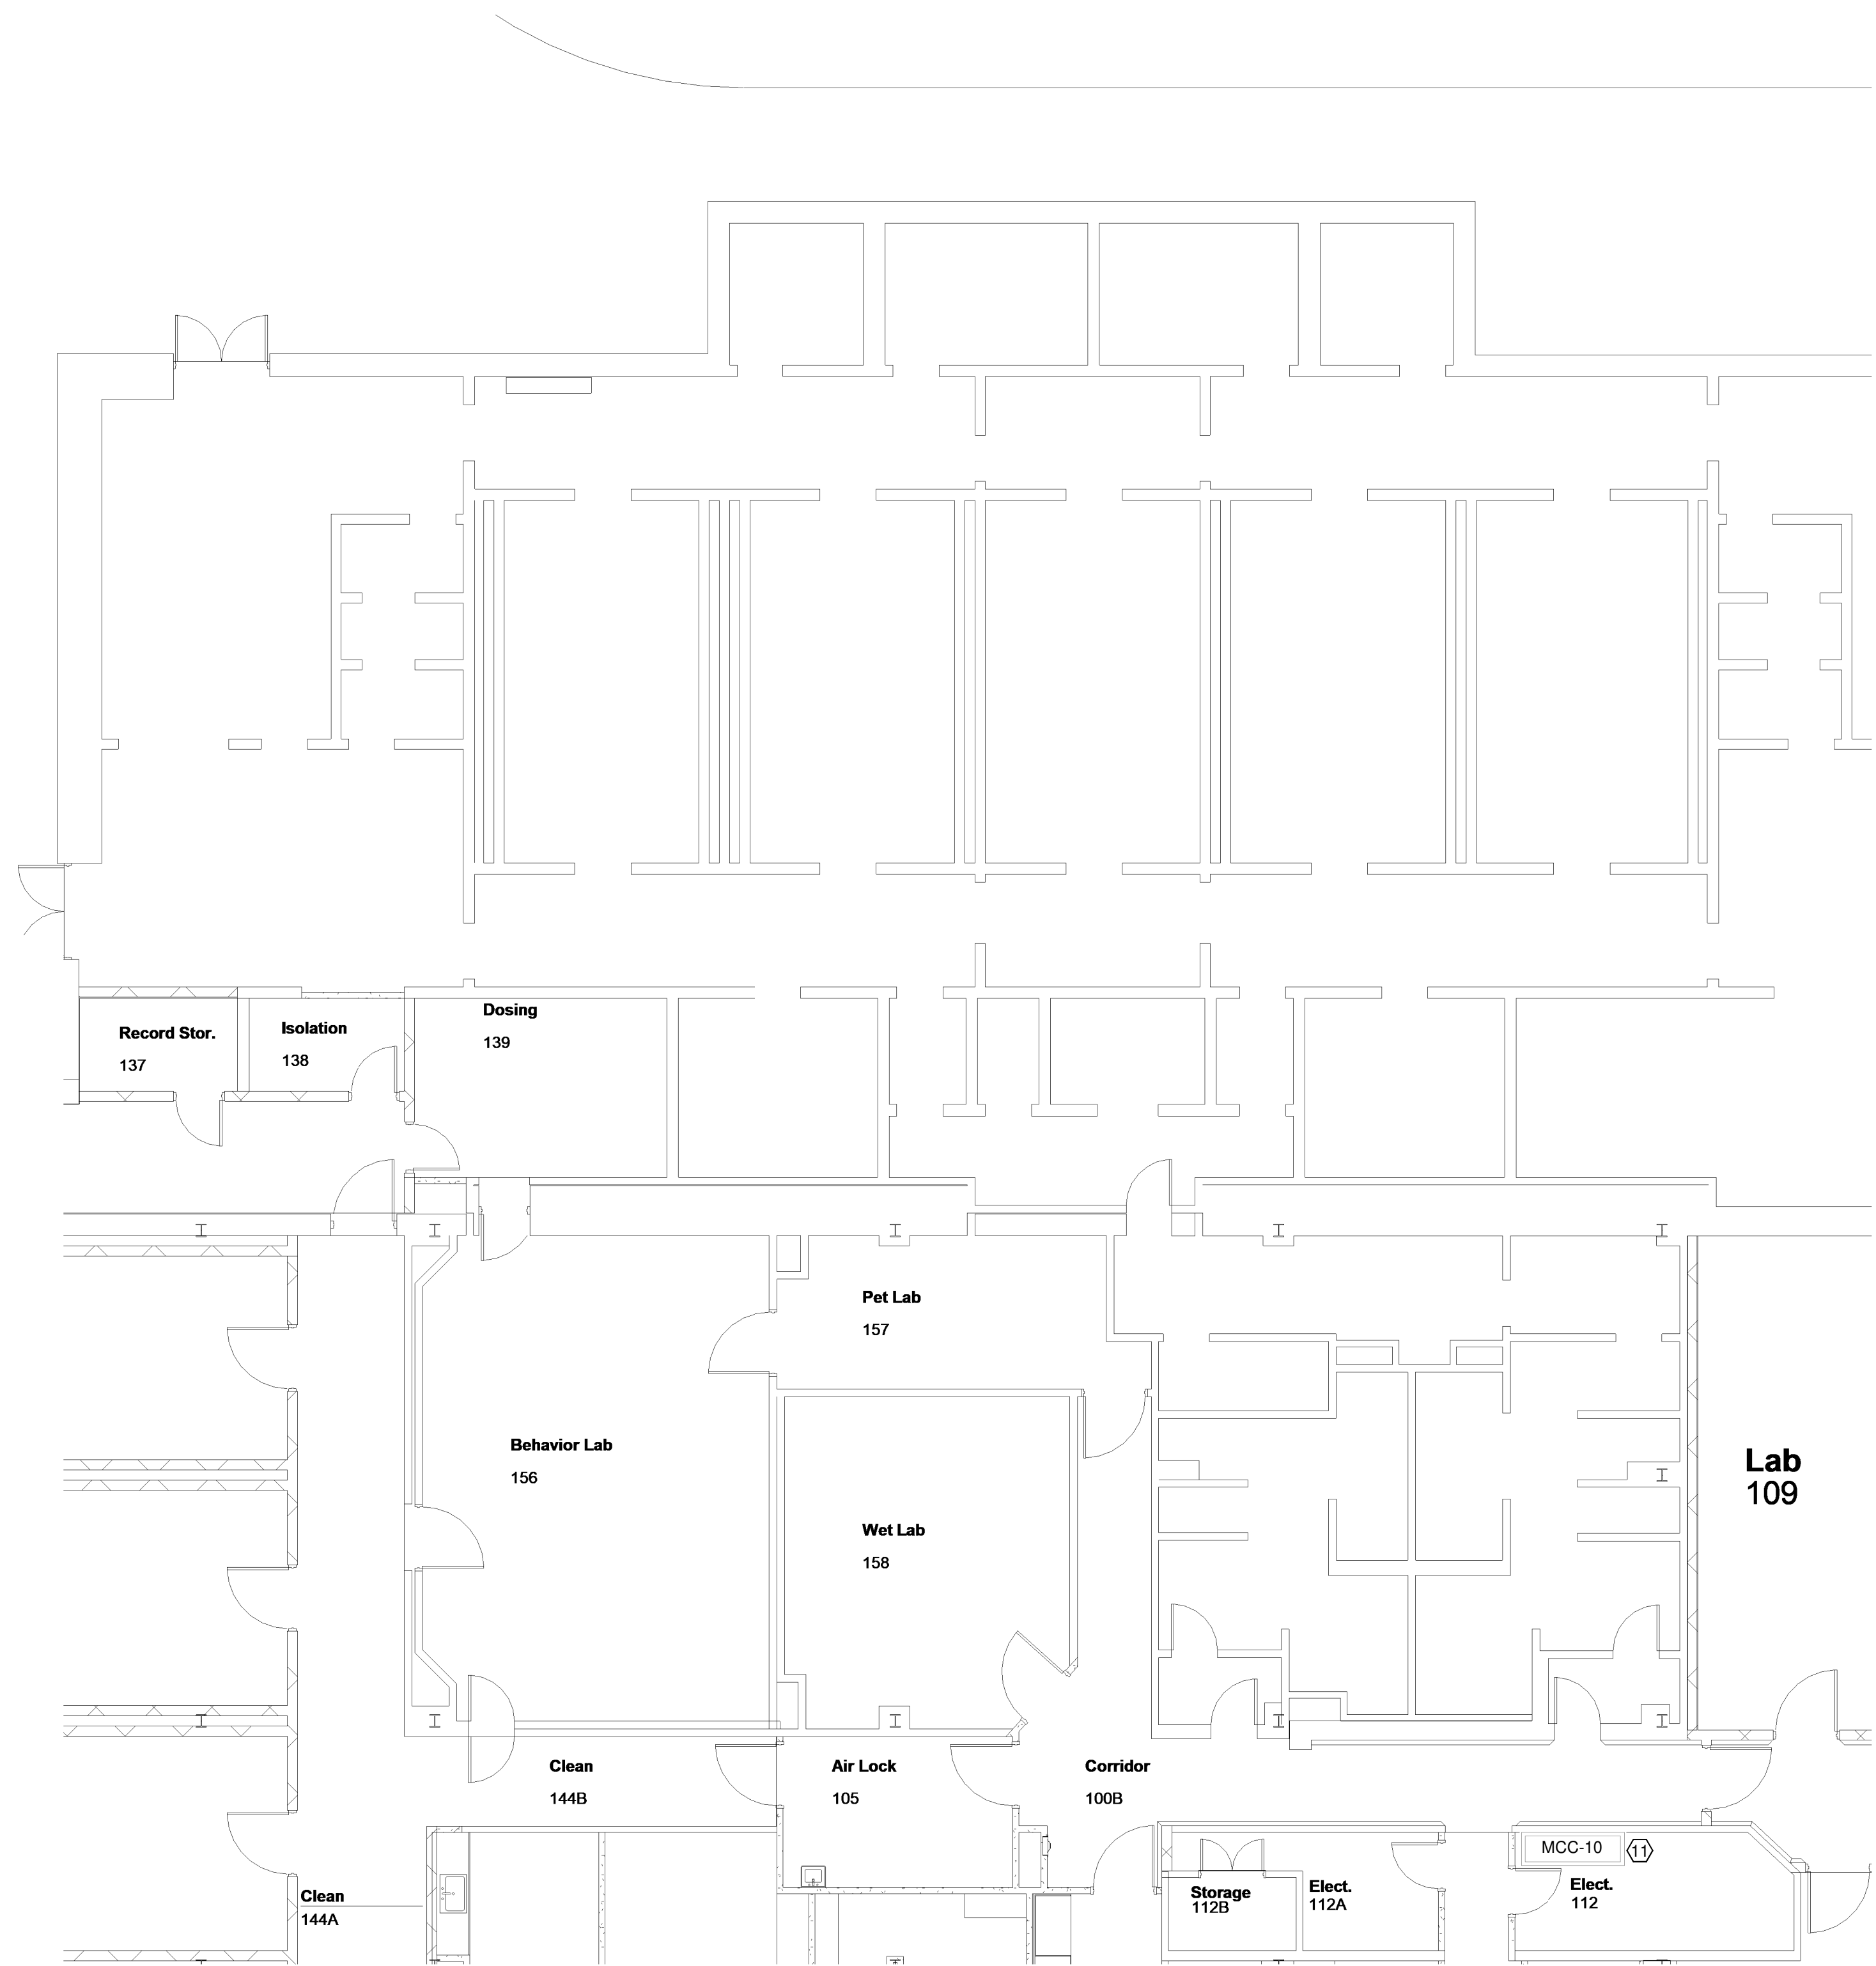

2 FLOOR PLAN - BUILDING 62 FIRST FLOOR - NEW

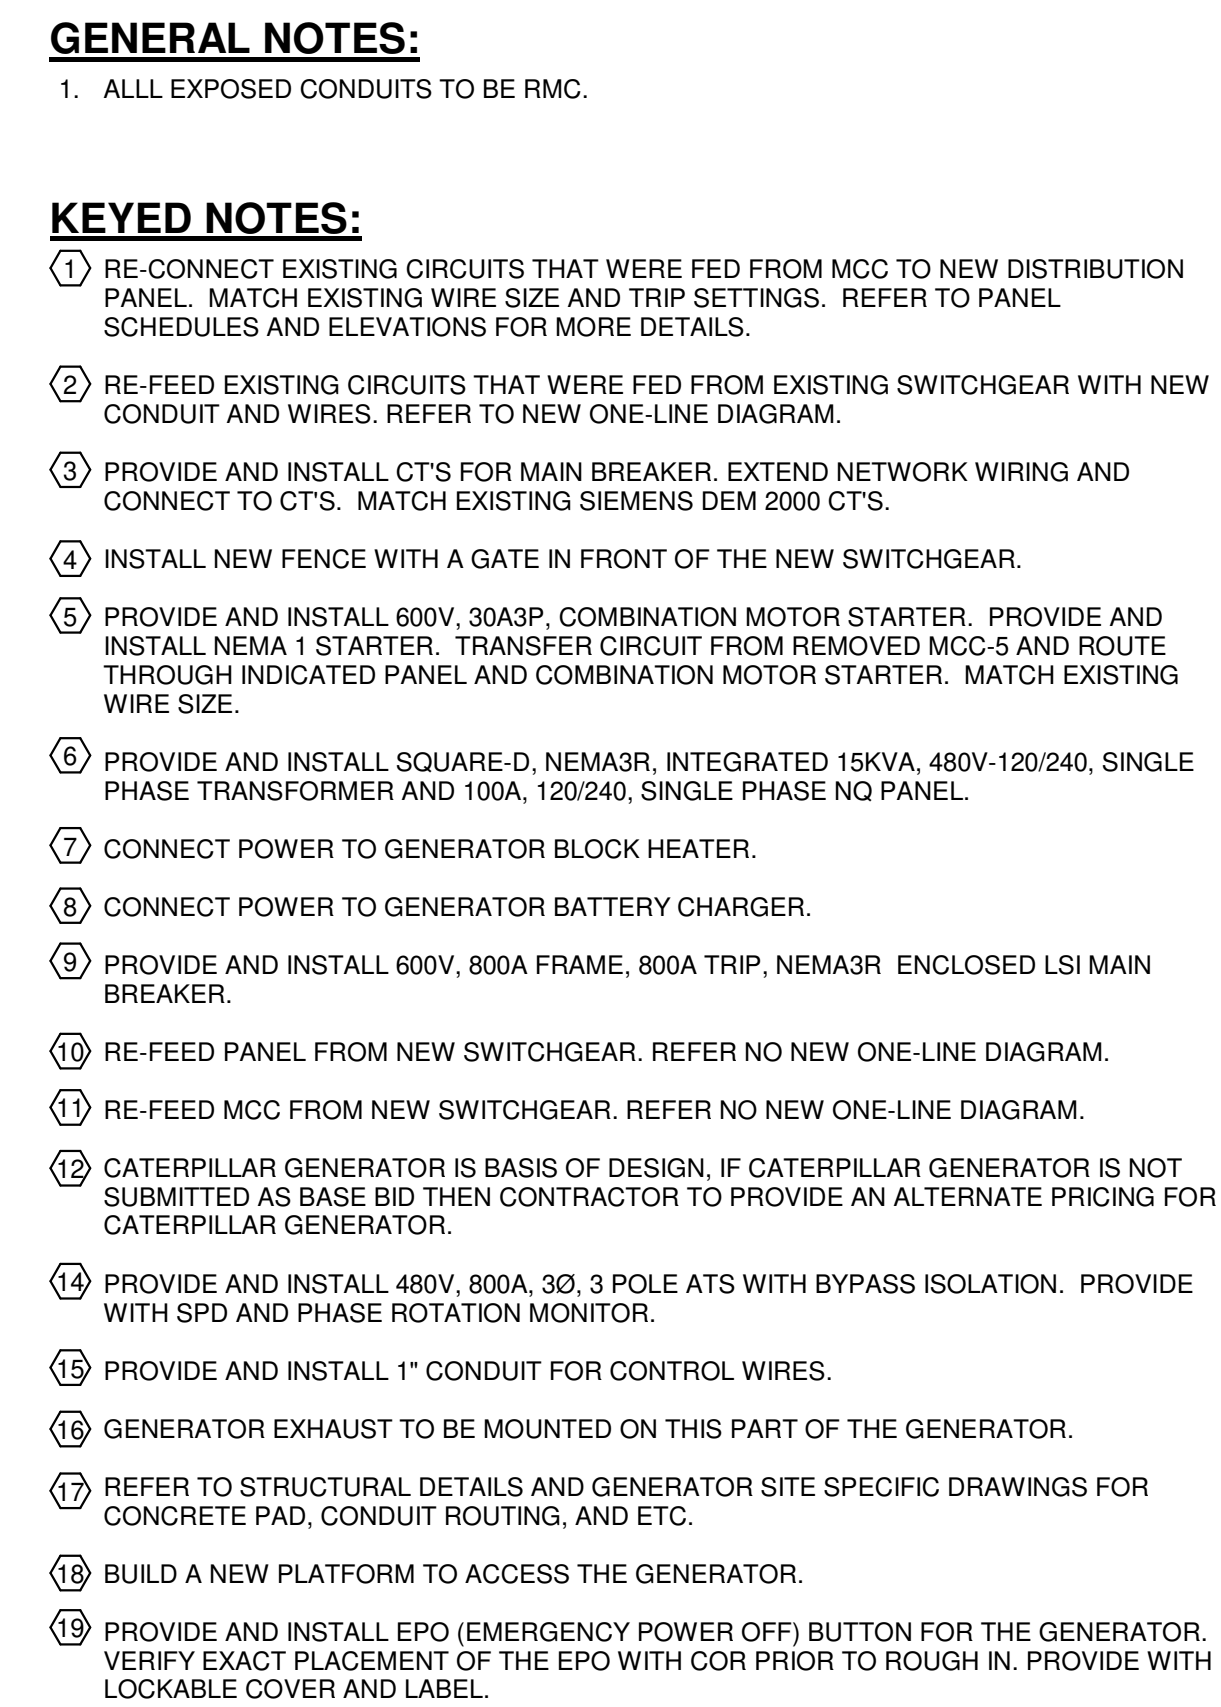

3 ONE-LINE DIAGRAM - BUILDING 62 NEW
NOT TO SCALE

[illegible]

MARK	DATE	DESCRIPTION
ISSUE DATE:		10-15-21
PROJECT NUMBER:		01-19-0062

SHEET TITLE:
**BUILDING 62 - FIRST &
BASEMENT FLOOR PLANS &
ONE-LINE DIAGRAM - NEW**

SHEET NUMBER:
E1220