



100% CONSTRUCTION DOCUMENTS

MCC BREAKER MAINTENANCE


JEFFERSON LABORATORIES
3900 NCTR ROAD, JEFFERSON, ARKANSAS 72079

MARK	DATE	DESCRIPTION
ISSUE DATE:	10-15-21	
PROJECT NUMBER:	01-19-0062	


SHEET TITLE:
**BUILDING 62 - FIRST &
BASEMENT FLOOR PLANS &
ONE-LINE DIAGRAM -
DEMOLITION**

SHEET NUMBER:

E1210

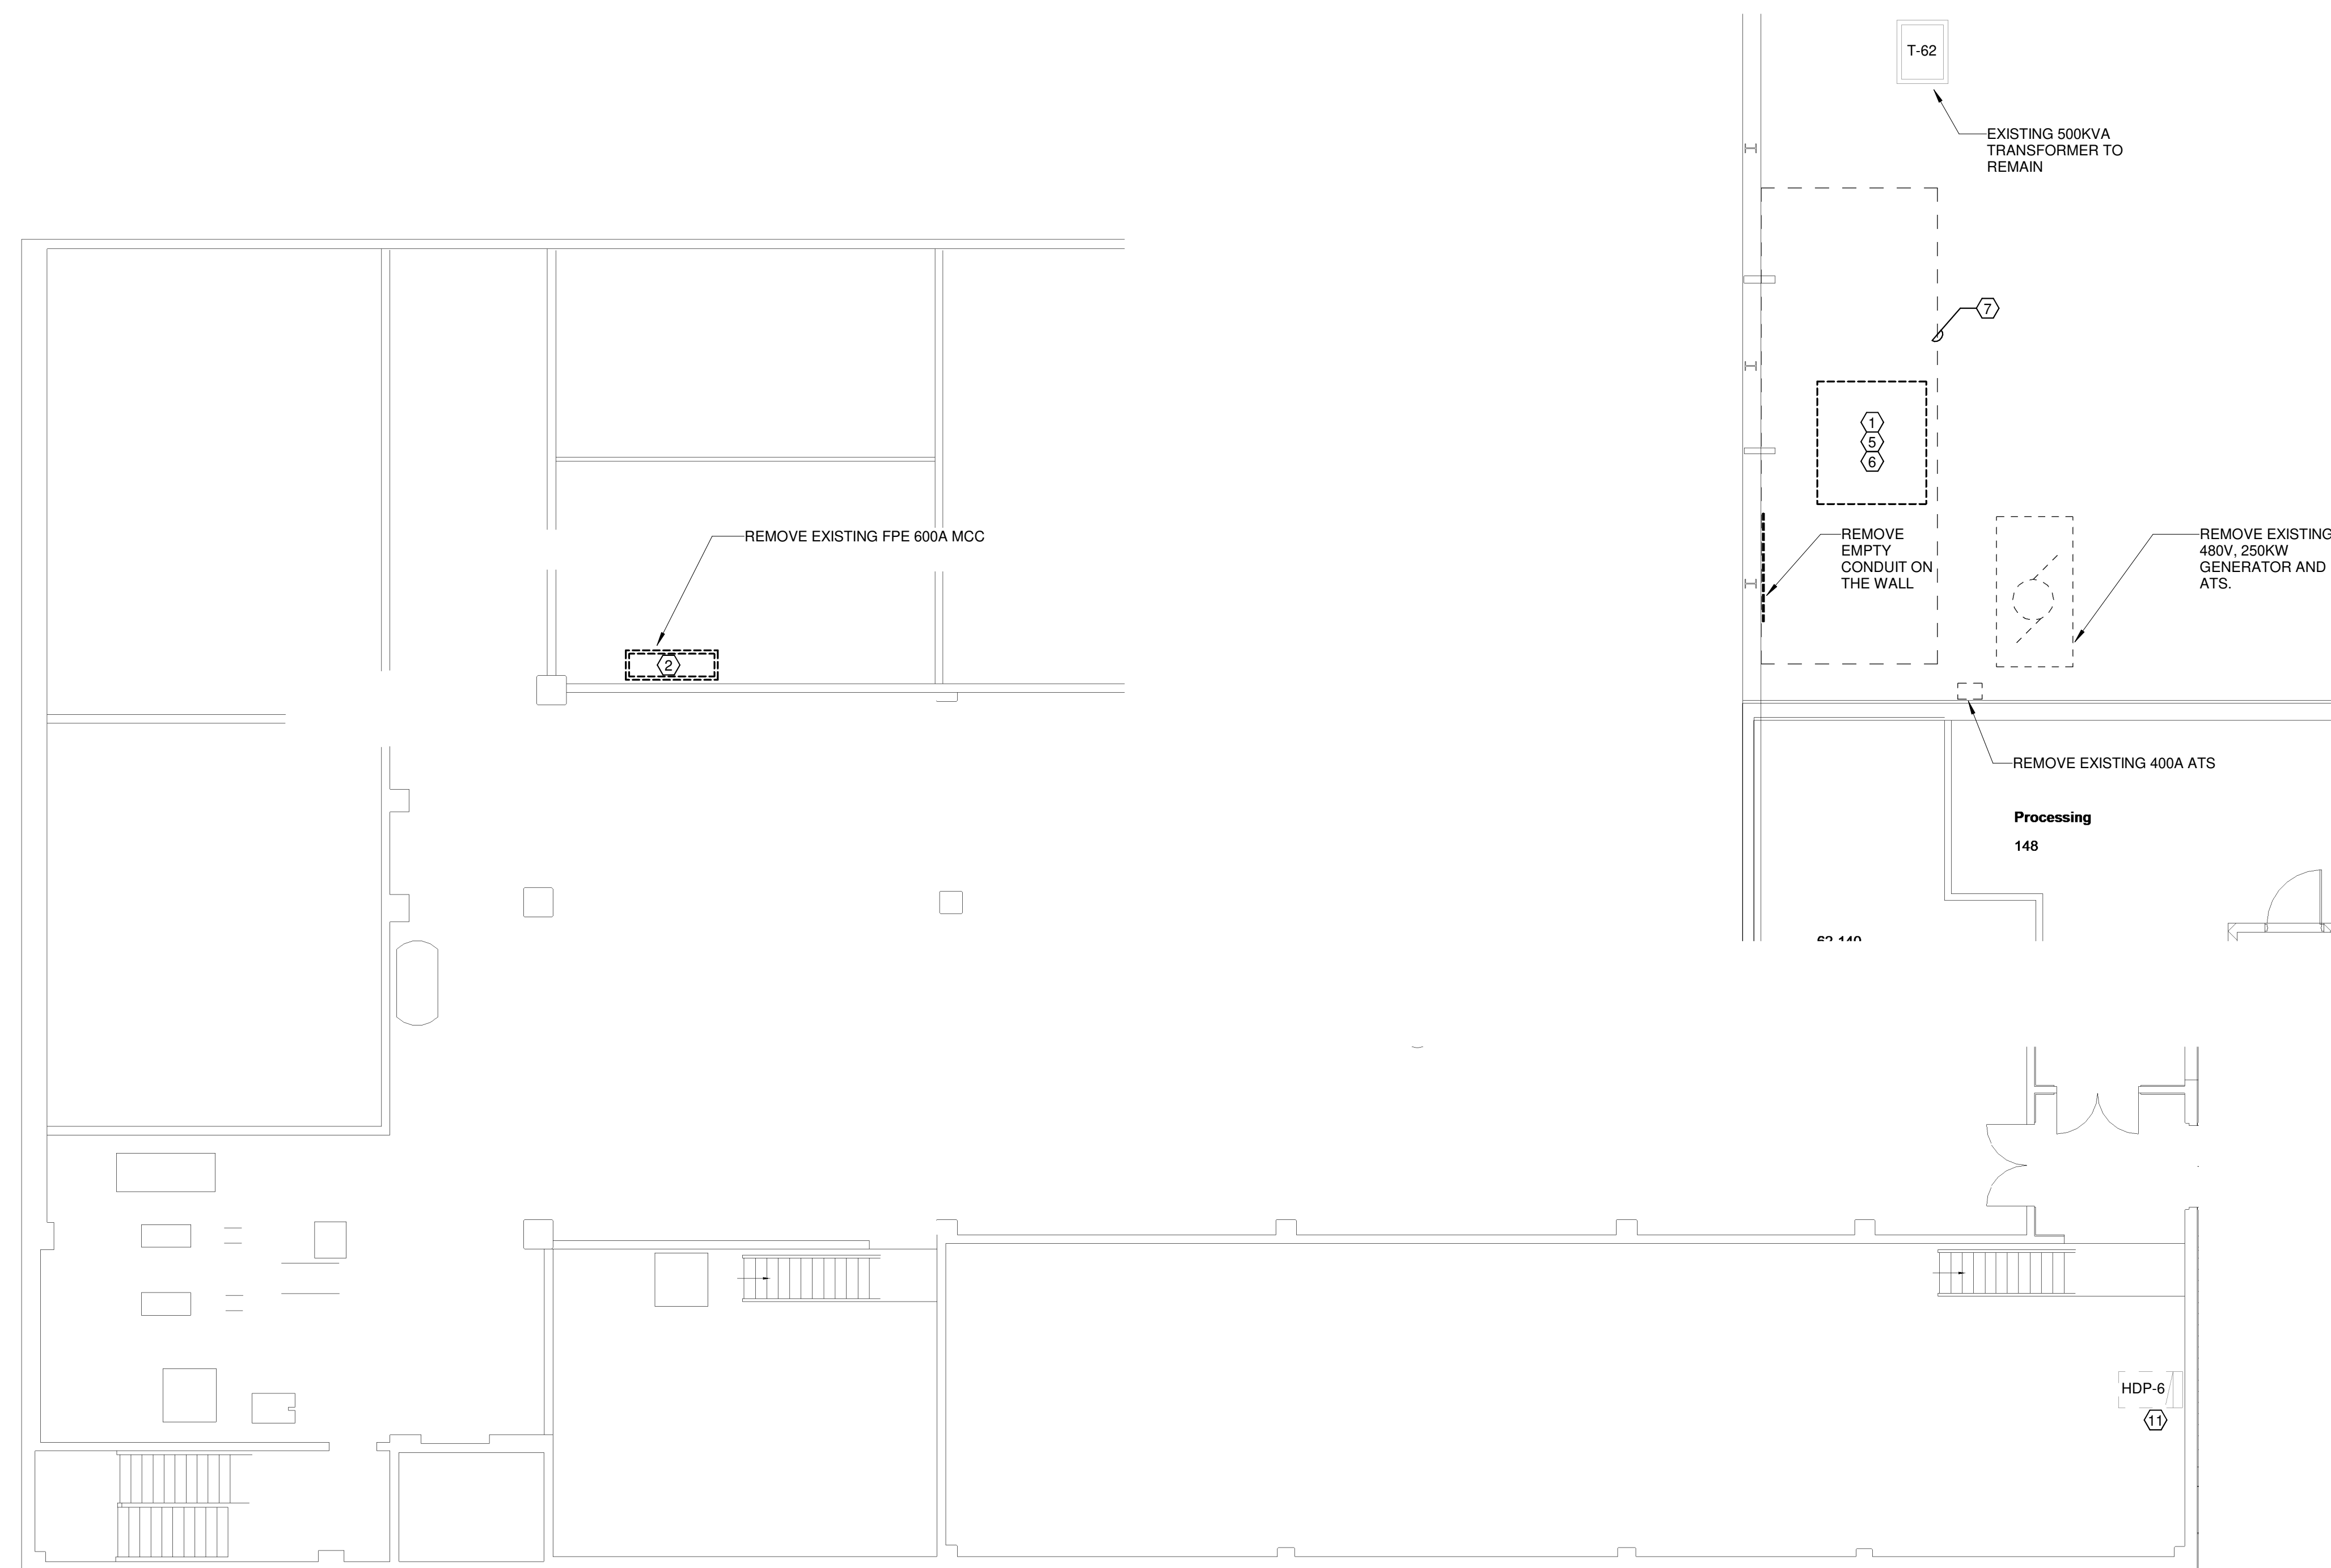

1 FLOOR PLAN - BUILDING 62 BASEMENT - DEMOLITION
1/8" = 1'-0"

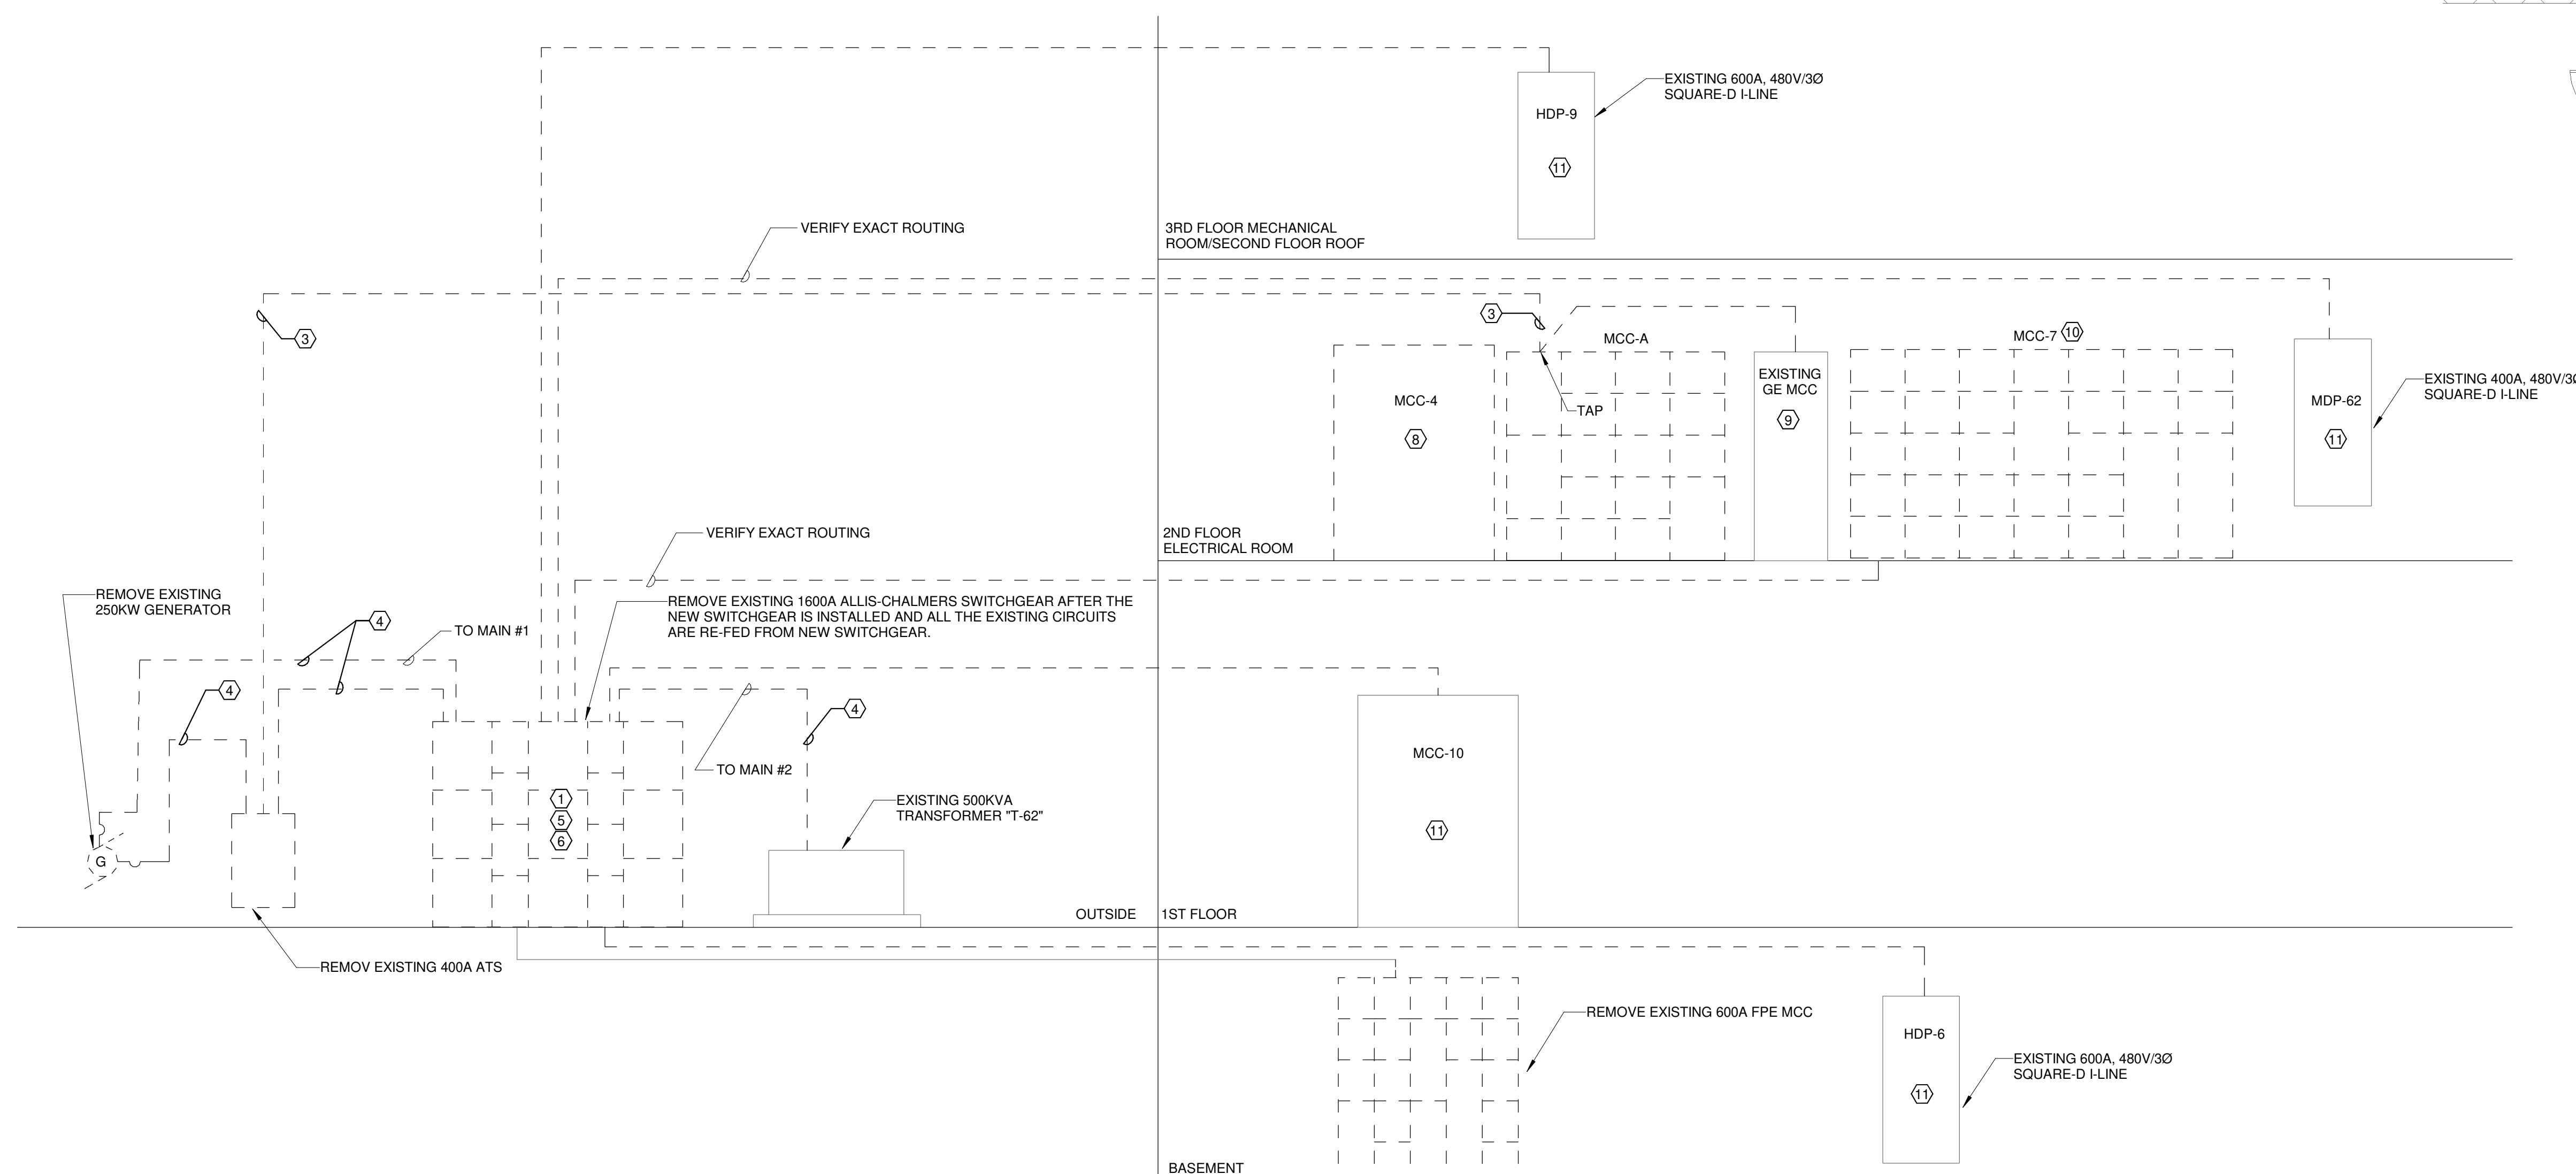

3 ONE-LINE DIAGRAM - BUILDING 62 DEMOLITION
NOT TO SCALE



② FLOOR PLAN - BUILDING 62 FIRST FLOOR - DEMOLITION
1/8" = 1'-0"

GENERAL NOTES:

1. UNLESS OTHERWISE NOTED, ALL ELECTRICAL EQUIPMENT TO REMAIN AND PROTECTED DURING CONSTRUCTION.
2. COORDINATE ALL POWER OUTAGES VERY CAREFULLY WITH OWNER MINIMUM OF 3 WEEKS IN ADVANCE PRIOR TO DISCONNECTING POWER.

DEMOLITION KEYED NOTES:

- ① REMOVE EXISTING SWITCHGEAR AFTER THE NEW SWITCHGEAR IS INSTALLED AND ALL THE EXISTING CIRCUITS ARE RE-FED FROM THE NEW SWITCHGEAR. REFER TO NEW FLOOR PLAN AND ELEVATIONS.
- ② EXISTING CIRCUITS FED OUT OF THE MCC TO BE RE-FED FROM NEW DISTRIBUTION PANEL. REFER TO ELEVATIONS AND NEW FLOOR PLAN.
- ③ REMOVE FEEDER AND MCC-A AFTER NEW DISTRIBUTION PANEL IS INSTALLED AND ALL THE CIRCUITS HAVE BEEN TRANSFERRED TO THE NEW PANEL. REFER TO NEW FLOOR PLAN AND ONE-LINE DIAGRAM.
- ④ REMOVE EXISTING FEEDER AFTER NEW SWITCHGEAR IS INSTALLED AND ALL THE CIRCUITS ARE RE-FED FROM NEW SWITCHGEAR.
- ⑤ ALL EXISTING CIRCUITS FED OUT OF THE SWITCHGEAR TO BE RE-FED FROM NEW SWITCHGEAR WITH NEW CONDUITS AND WIRES. REFER TO ELEVATIONS AND NEW FLOOR PLAN.
- ⑥ PROTECT NETWORK WIRING FOR CT'S, EXTEND AND CONNECT TO THE NEW SWITCHGEAR.
- ⑦ REMOVE/MODIFY FENCE FOR NEW SWITCHGEAR. REFER TO NEW FLOOR PLAN.
- ⑧ REMOVE DECOMMISSIONED MCC-4.
- ⑨ EXISTING GE MCC TO REMAIN AND RE-FED FROM NEW DISTRIBUTION PANEL. REFER TO NEW FLOOR PLAN. REMOVE EXISTING FEEDER AFTER MCC IS RE-FED.
- ⑩ REMOVE FEEDER AND MCC-7 AFTER NEW DISTRIBUTION PANEL IS INSTALLED AND ALL THE CIRCUITS HAVE BEEN TRANSFERRED TO THE NEW PANEL. REFER TO NEW FLOOR PLAN AND ONE-LINE DIAGRAM.
- ⑪ EXISTING PANEL/MCC TO REMAIN AND PROTECTED DURING CONSTRUCTION. PANEL TO BE RE-FED FROM NEW SWITCHGEAR. REMOVE EXISTING FEEDER AFTER PANEL IS RE-FED FROM NEW SWITCHGEAR. REFER TO NEW FLOOR PLAN AND ONE-LINE DIAGRAM.