

D

C

B

A


D

C


UNCLASSIFIED

B

A

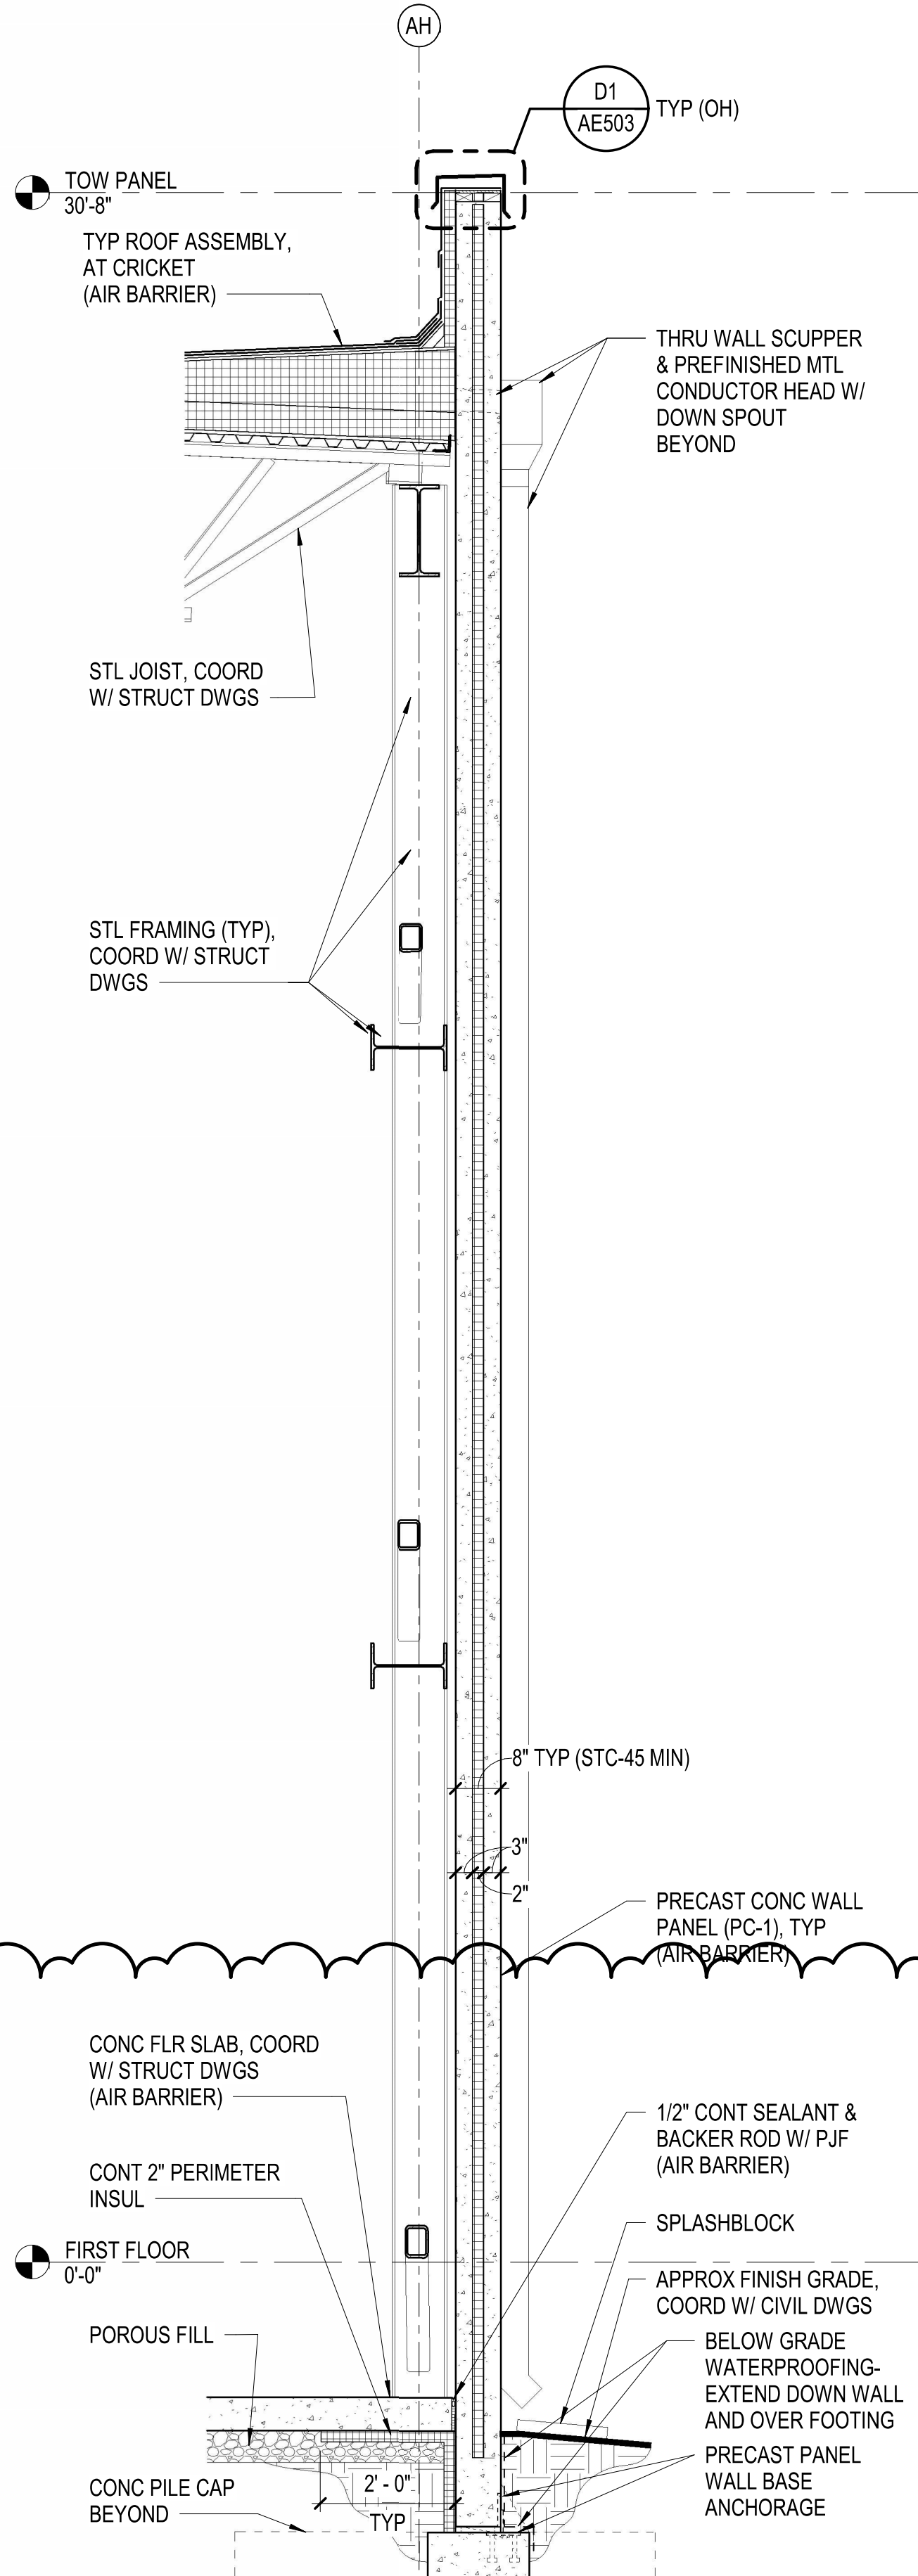

B5 AE301 **A1** WALL SECTION
1/2" = 1'-0" TYP WALL SECTION

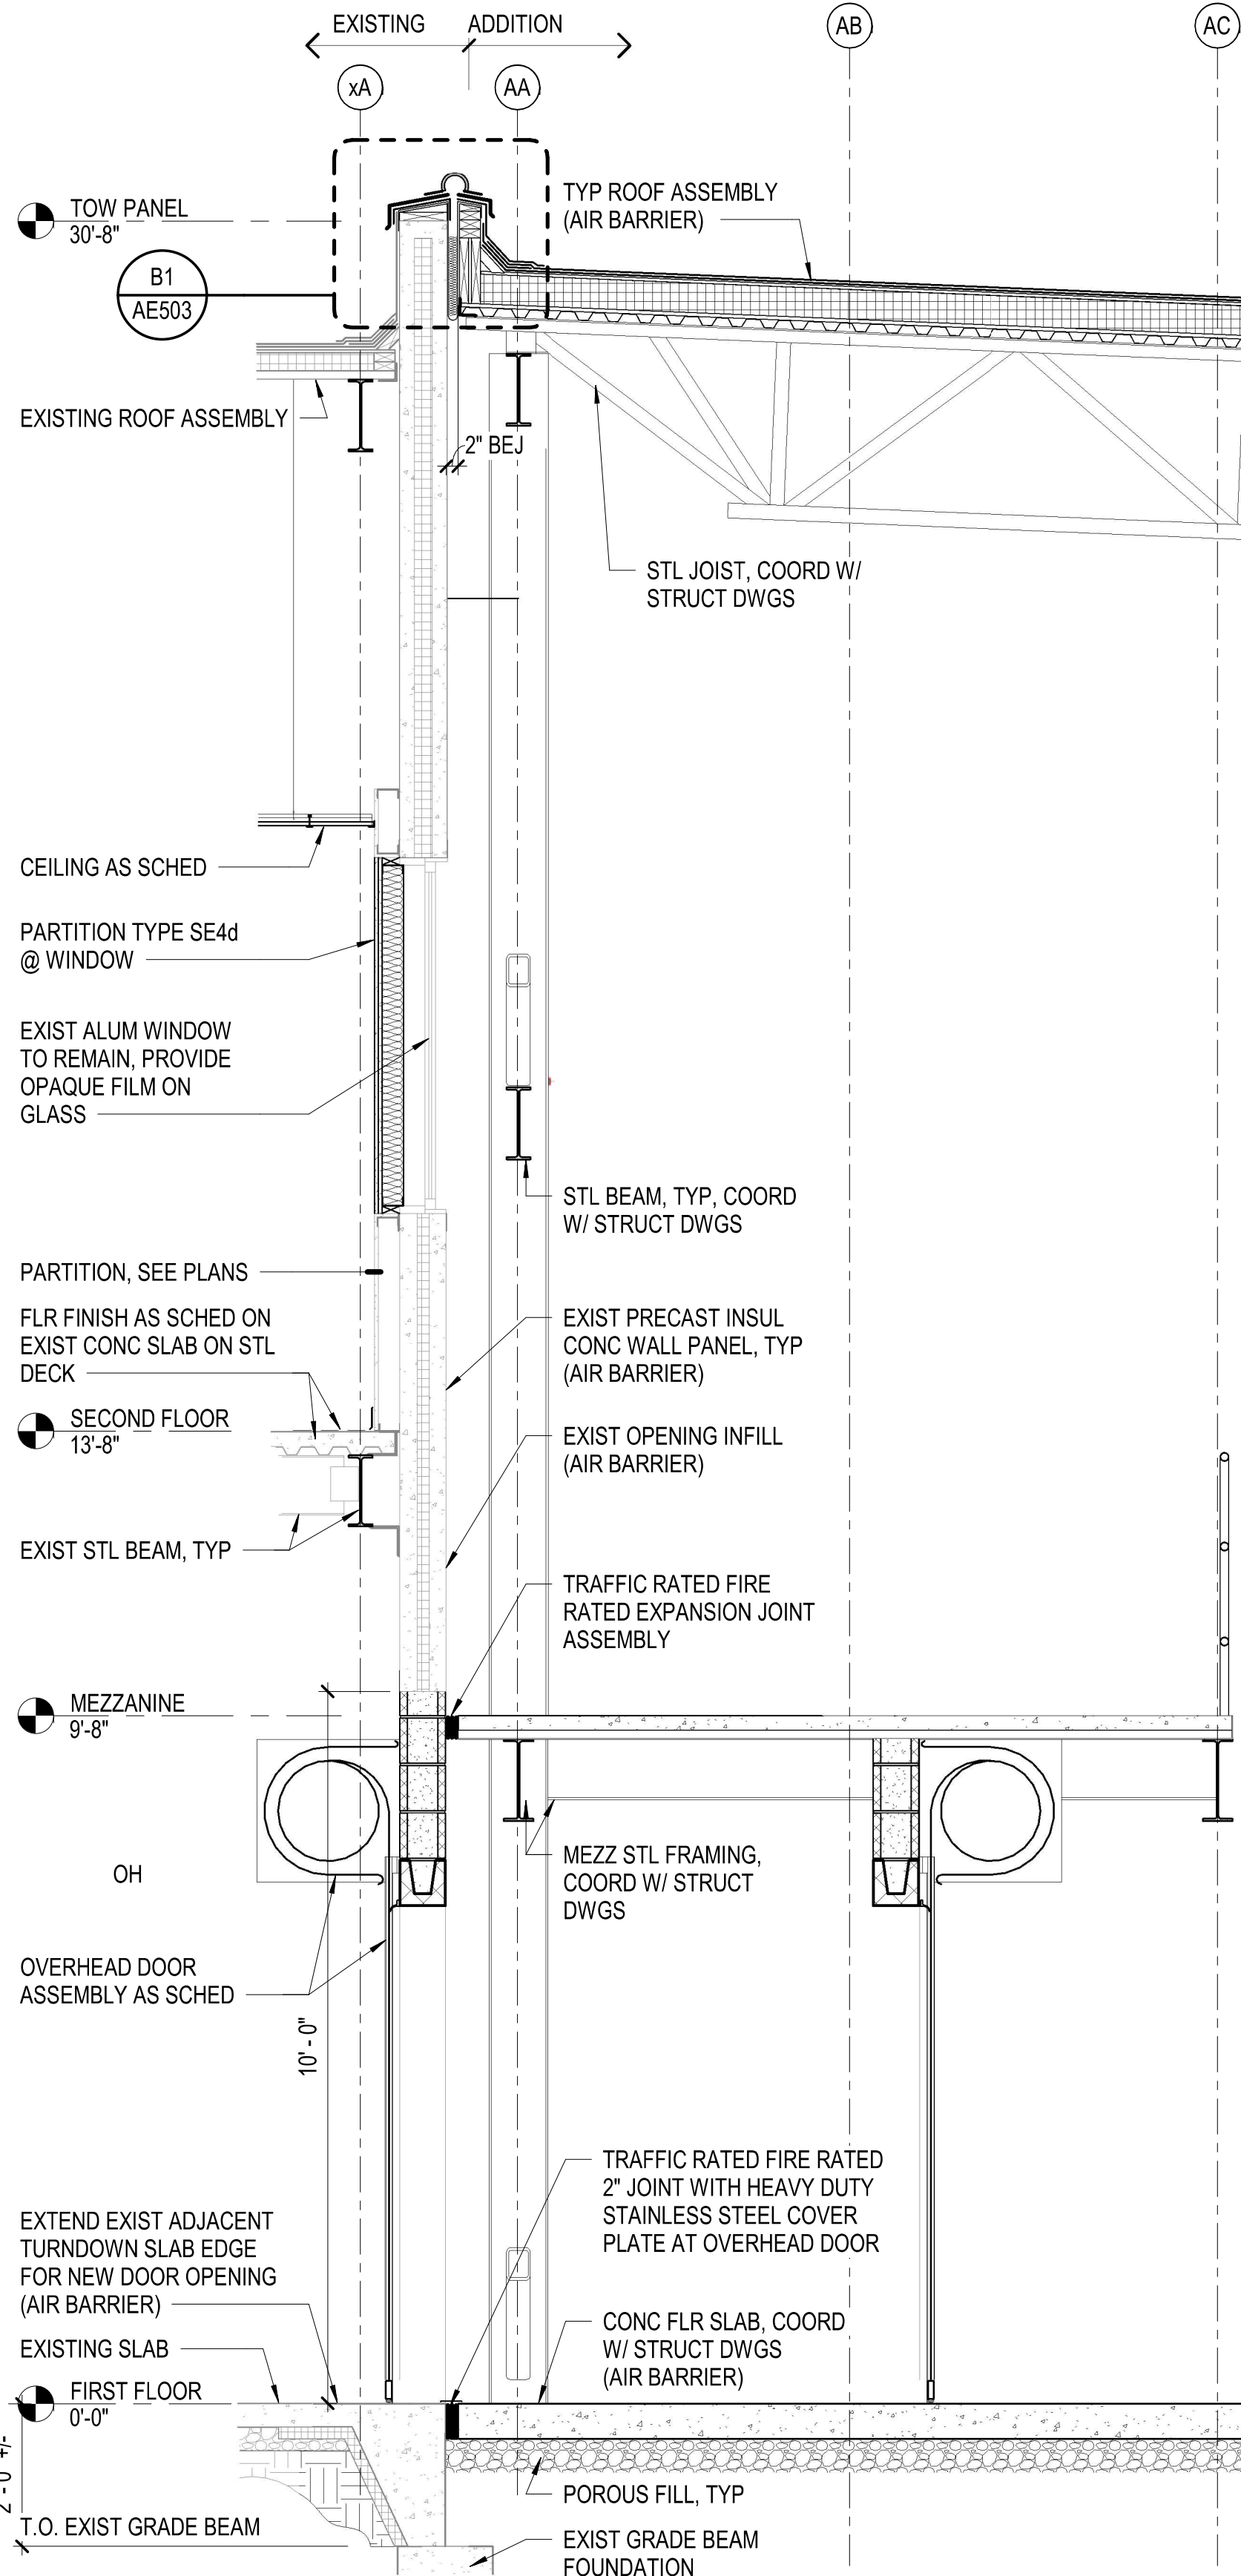

D4 AE103 **A2** WALL SECTION
1/2" = 1'-0" AT HIGH BAY 128 WEST WALL

GENERAL NOTES THIS SHEET ONLY

- A. REFER TO EXTERIOR COLOR LEGEND ON SHEET A-001 FOR MATERIAL COLOR ASSIGNMENTS.
- B. PRECAST CONCRETE WALL PANEL REINFORCING & CONNECTIONS ARE A DELEGATED DESIGN RESPONSIBILITY OF THE WALL PANEL MANUFACTURER.
- C. REFER TO STRUCTURAL DRAWINGS FOR CAST-IN-PLACE CONCRETE STRUCTURE REINFORCING INFORMATION NOT SHOWN ON THIS SHEET.
- D. UTILITY EQUIPMENT, ASSEMBLIES, PIPING / DUCTS, ETC ARE NOT SHOWN ON THIS SHEET FOR CLARITY, COORDINATE WITH DISCIPLINE DRAWINGS ACCORDINGLY.
- E. REFER TO SHEET AE503 FOR ROOF TYPICAL DETAILS.
- F. EXPOSED EXISTING & NEW PRECAST CONCRETE WALL PANELS TO BE PREPARED & PAINTED WITH ELASTOMERIC PAINT COATING, COLOR TO MATCH EXISTING BUILDING FINISH ("SAND") COLOR.

GRAPHIC SCALE(S)



DATE	DESCRIPTION	SYN	REVISIONS	DATE	APPR
12/25/25			2		



CLARKNEXSEN
A JMT Company
4525 MAIN STREET
SUITE 1400
VIRGINIA BEACH, VA 23462
757-455-5800 FAX 757-455-5638
WWW.CLARKNEXSEN.COM

APPROVED	AE INFO
FOR COMMANDER NAVFAC	
ACTIVITY	Approved by Don Bryant, PE, N10 Facilities Engineer, NSWDG via Email
SATISFACTORY TO DATE	07/09/2025
DES	DJH
BRW	JWL
CHK	RAM
PMOM	JT/SW
BRANCH MANAGER	DJD
CHIEF ENGINEER	JWL
FIRE PROTECTION	HPN

DEPARTMENT OF THE NAVY
NAVAL FACILITIES ENGINEERING SYSTEMS COMMAND
NAVAL FACILITIES ENGINEERING SYSTEMS COMMAND - MID-ATLANTIC
NAVAL STATION - NORFOLK, VA
NAS OCEANA, DAM NECK ANNEX
Q-1075 SOF OPERATIONS BUILDING ADDITION
VIRGINIA BEACH, VA

SCALE: AS NOTED
PROJECT NO.: 1625040
CONSTR. CONTR. NO. N40085-19-D-9041
NAVFAC DRAWING NO. 12928991
SHEET 86 OF 239
AE302