

1

2

3

UNCLASSIFIED

4

5

D

C

B

A

D

C

B

A

GENERAL NOTES

1. REFER TO DRAWING P-001 FOR LEGENDS, ABBREVIATIONS AND GENERAL NOTES.
2. ALL PIPING IS EXISTING TO REMAIN UNLESS OTHERWISE NOTED.
3. EXISTING COMPRESSED AIR DISTRIBUTION PIPING TO REMAIN UNLESS OTHERWISE NOTED.

NEW WORK NOTES

- 1 CONNECT WATER PIPING TO EXISTING WATER PIPING AT APPROXIMATE LOCATION INDICATED.
- 2 CONNECT SANITARY WASTE PIPING TO EXISTING SANITARY WASTE PIPING AT APPROXIMATE LOCATION INDICATED.
- 3 PROVIDE 3/4" COMPRESSED AIR DROP FOR CAR LIFT. PROVIDE REGULATOR, FILTER AND COMPRESSED AIR TEE FITTING. COORDINATE EXACT CONNECTION REQUIREMENTS WITH EQUIPMENT PROVIDED.




CLARKNEXSEN
A JMT Company
4525 MAIN STREET
SUITE 1400
VIRGINIA BEACH, VA 23462
757-455-5800 FAX 757-455-5638
WWW.CLARKNEXSEN.COM

FOR COMMANDER NAVFAC
ACTIVITY
Approved by Don Bryant, PE, N10
Facilities Engineer, NSWDG
via Email
SATISFACTORY TO DATE 07/09/2025
DES MDD BRW MDD CHK JBW
PMOM JT/SW
BRANCH MANAGER ALG
CHIEF ENGINEER JWJ
FIRE PROTECTION HPN


NAVAL FACILITIES ENGINEERING SYSTEMS COMMAND
NAVAL FACILITIES ENGINEERING SYSTEMS COMMAND - MID-ATLANTIC
NAVAL STATION - NORFOLK VA
NAS OCEANA, DAM NECK ANNEX
Q-1075 SOF OPERATIONS BUILDING ADDITION

FIRST FLOOR PLAN AREA A

KEY PLAN

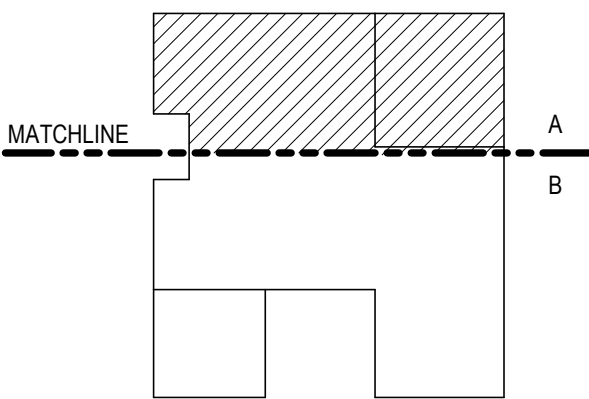

GRAPHIC SCALE(S)

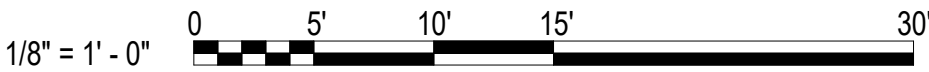

SCALE: AS NOTED
EPROJCT NO.: 1625040
CONSTR. CONTR. NO. N40085-19-D-9041
NAVFAC DRAWING NO. 12929036
SHEET 131 OF 239

PL102

DRAWING REVISION: 25 AUGUST 2020

1

2

3

UNCLASSIFIED

4

5

D

C

B

A

D

C

UNCLASSIFIED

B

A

GENERAL NOTES

- 1. REFER TO DRAWING P-001 FOR LEGENDS, ABBREVIATIONS AND GENERAL NOTES.
- 2. ALL PIPING IS EXISTING TO REMAIN UNLESS OTHERWISE NOTED.
- 3. EXISTING COMPRESSED AIR DISTRIBUTION PIPING TO REMAIN UNLESS OTHERWISE NOTED.

NEW WORK NOTES


- 1. PROVIDE SINK (P-4) AND THERMOSTATIC MIXING VALVE. CONNECT TO EXISTING WASTE AND WATER WATER SUPPLY AND SHUTOFF.
- 2. CONNECT FRIDGE TO EXISTING FRIDGE WATER LINE AT LOCATION INDICATED.
- 3. PROVIDE WATER SUPPLY BOX FOR COFFEE MAKER.




CLARK NEXSEN
A JMT Company
4525 MAIN STREET
SUITE 1400
VIRGINIA BEACH, VA 23462
757-455-5800 FAX 757-455-5638
WWW.CLARKNEXSEN.COM

APPROVED			
FOR COMMANDER NAVFAC			
ACTIVITY Approved by Don Bryant, PE, N10 Facilities Engineer, NSWDG via Email			
SATISFACTORY TO DATE 07/09/2025			
DES	MDD	BRW	MDD
PMOM	JT/SW		
BRANCH MANAGER	ALG		
CHIEF ENGINEER	JWJ		
FIRE PROTECTION	HPN		

KEY PLAN

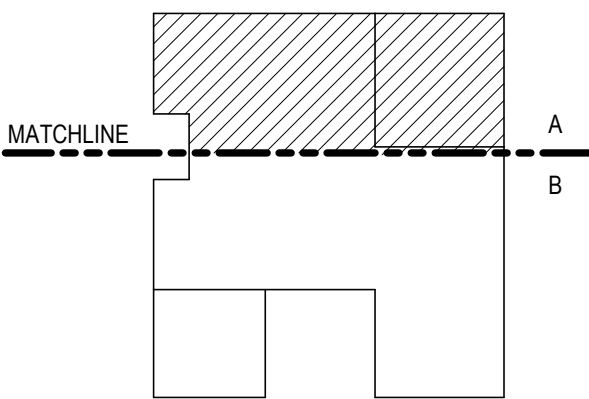


GRAPHIC SCALE(S)

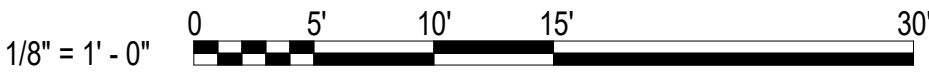

SCALE: AS NOTED	
PROJECT NO.:	1625040
CONSTR. CONTR. NO.	N40085-19-D-9041
NAVFAC DRAWING NO.	12929038
SHEET 133 OF 239	

PL104

DRAWING REVISION: 25 AUGUST 2020

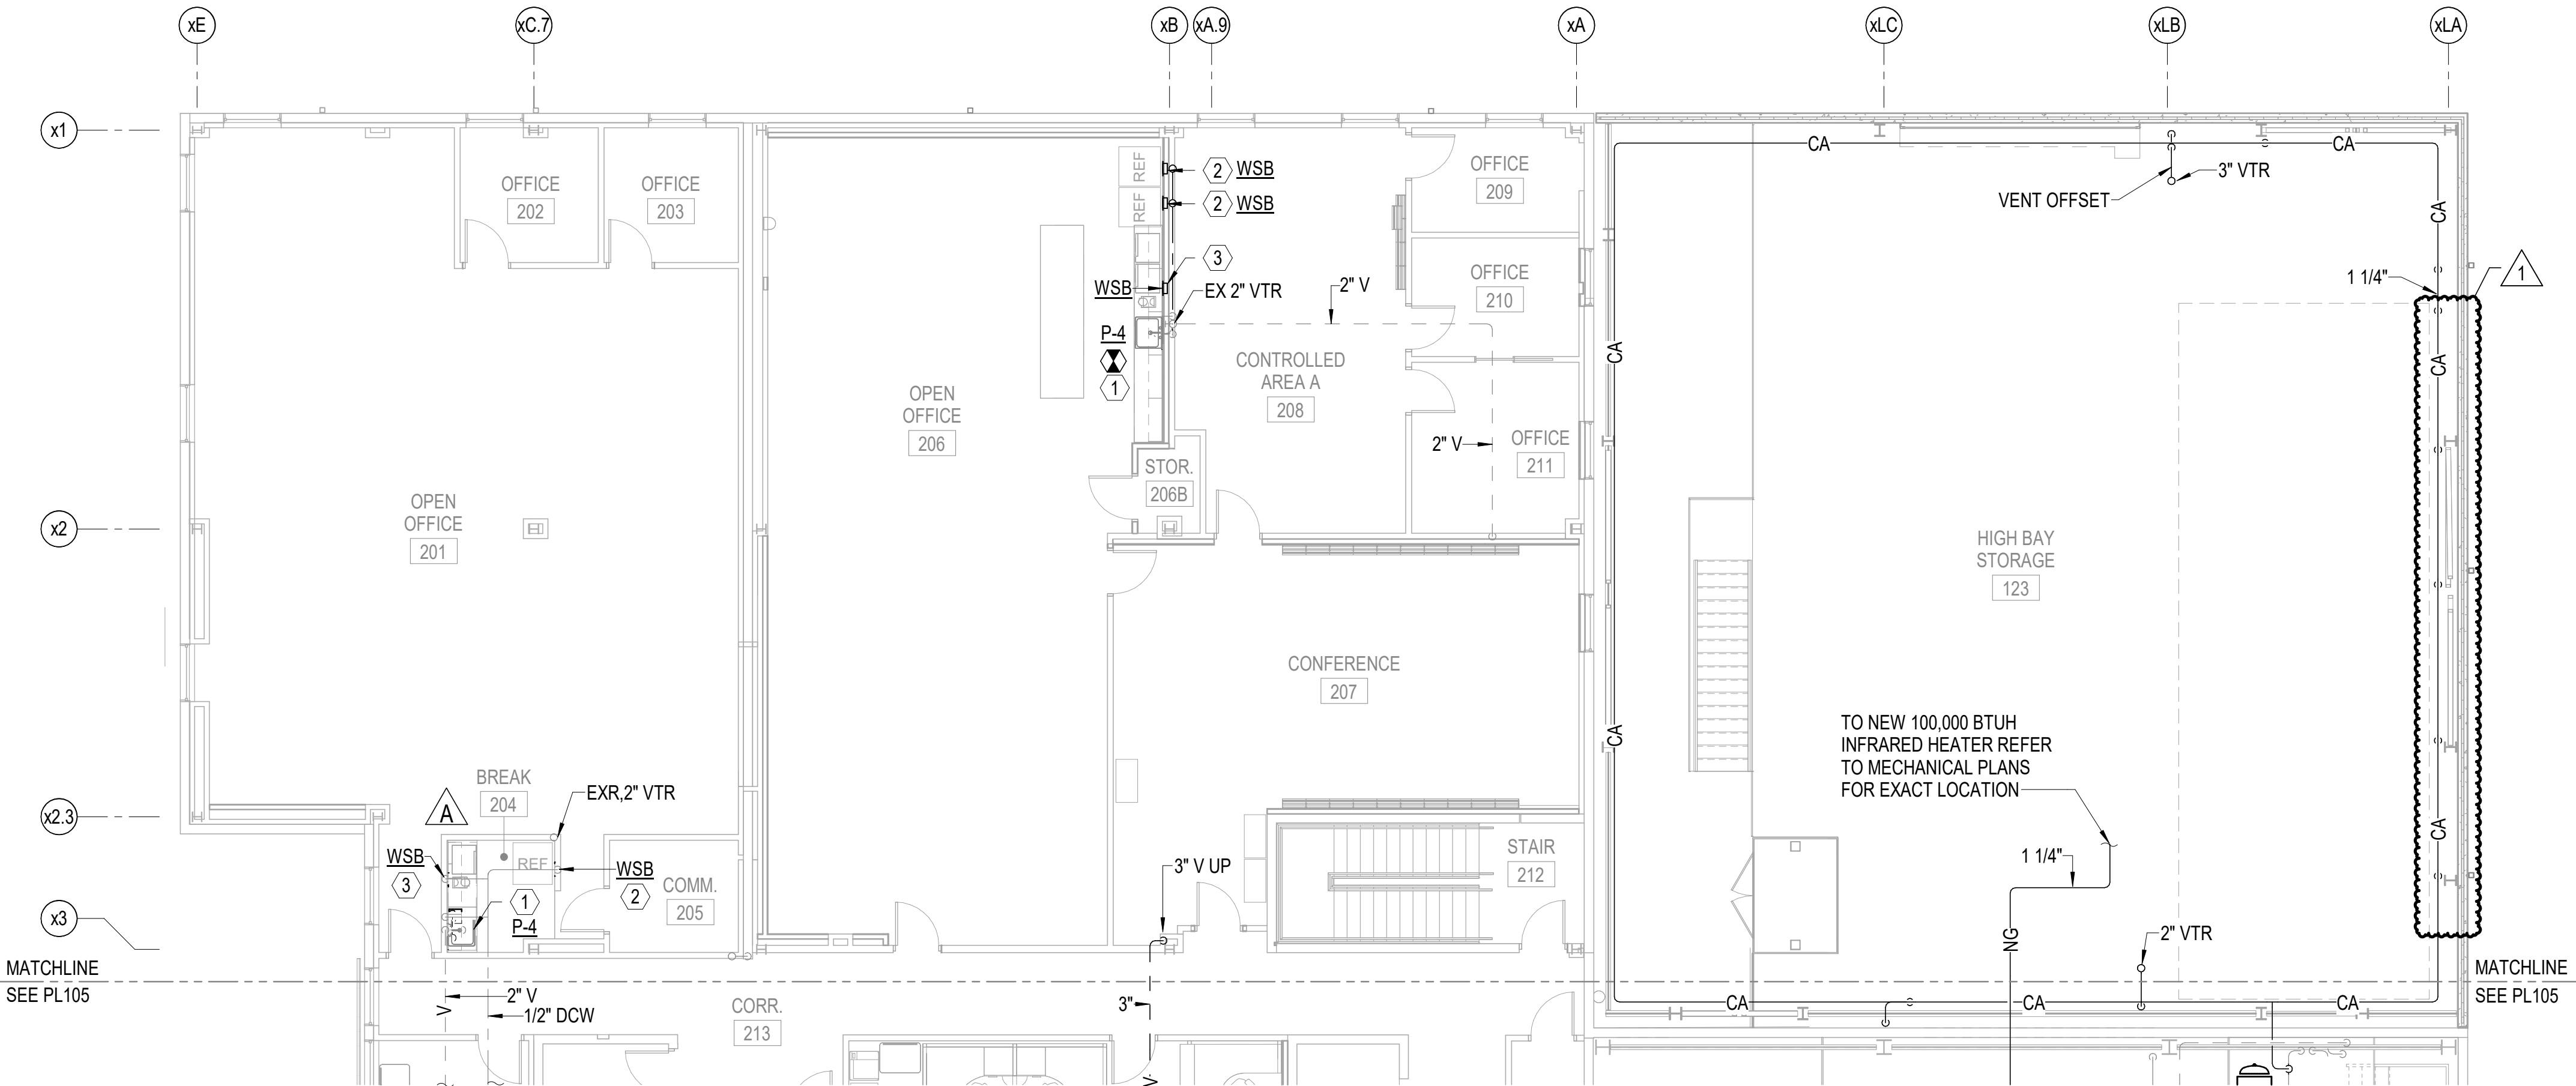

SECOND FLOOR AREA A
1/8" = 1'-0"