

## Project #4: MDC-PAC Modular SCIF

## **Project Title: MDC-PAC Modular SCIF**

### **1.0 DESCRIPTION OF WORK**

Provide all plant, labor, tools, equipment, and materials to perform all work in strict accordance with the specifications and plans required for the project. The Contractor shall accomplish all items of work needed to provide a complete and usable SCIF-in-a-Box (SIAB) system. All work must adhere to the applicable drawings, specifications, and relevant national, state, and local codes and standards.

### **2.0 AREA DESCRIPTION**

The work will occur at the designated project site at Joint Base Lewis-McChord. The Contractor is responsible for verifying all site conditions, including the availability of electrical and communication services at the designated tie-in points.

### **3.0 PRINCIPAL ITEMS TO BE ACCOMPLISHED**

#### **3.1 Site Work and Foundation**

- Concrete Pad Installation:
  - Excavate and prepare the site for a new concrete pad at the location of the new SCIF in a box.
  - Prepare the subgrade and install a crushed aggregate base course, compacted to 95% standard density. The contractor shall provide a compaction test as a submittal.
  - Pour a new 6" thick, 4,000 psi Portland cement concrete pad. The pad shall have a 1" chamfer on all edges and extend 4" above the surrounding grade. Concrete pad requirements may change based on requirements of the SCIF in a box.
  - The concrete pad shall have a thickened edge extending 12" below grade. Both the pad and thickened edge shall be reinforced with #4 rebar at 12" O.C. in each direction.
  - The contractor shall provide a concrete mix design submittal and the 28-day compressive strength test results.
- SIAB Procurement & Placement:
  - Modular Unit shall be approximately 1,000 SF, provide space for approximately 23-25 workstations, and shall meet ICD 705 and SAPF requirements

- Mount and secure the SCIF in a box onto the newly installed concrete pad per the manufacturer's anchoring requirements.
- The contractor is responsible for procuring the machinery necessary to lift and place the SIAB.
- Provide stub-out locations in the concrete pad for electrical and communications services.

### 3.2 Electrical Service

- Conduit and Wiring:
  - Install appropriately sized electrical service to provide 120/208V, 3-phase, 4-wire, 200A, 60 Hz service to the SIAB. Electrical service demands will be driven by chosen SCIF in a box requirements.
  - Trench and install conduit from the Main Distribution Panel in Building 4290 to the SIAB's electrical panel stub-out location.
  - All conductors used shall be copper and must be continuous runs without splices. All exterior fittings shall be weatherproof.
- Connections and Testing:
  - Provide and install a new 200A breaker in the designated distribution panel.
  - Provide electrical grounding to the SIAB mounted bonding plate per the project specifications.
  - Connect the electrical service to the SIAB and coordinate with the government Project Manager (PM) for a full systems check.
  - Perform an arc flash study for the affected electrical equipment and provide warning labels. Provide the study results as a submittal.

### 3.3 Communications Infrastructure

- Duct Bank Installation:
  - Install a duct bank system from the designated communications tie-in point (e.g., existing manhole or hand hole) to the SIAB's communications panel stub-out.
  - Install a new telecommunications maintenance hole, if required by the project design.


- The duct system shall be concrete-encased schedule-40 conduit. The contractor is responsible for field-verifying all measurements.
- Cable and Service Installation:
  - Engineer-Furnish-Install-and-Test (EFI&T) a complete and usable telecommunications fiber optic and copper cable system.
  - Install new single-mode (SM) fiber optic and multi-pair copper cabling from the source at Building 4290 to the SIAB, using the new duct bank infrastructure.
  - Fusion splice new fiber cables as required and install new splice cases.
  - Install new fiber patch panels (Lightguide Interconnection Units or LIUs) and a telecommunications equipment cabinet inside the SIAB.
  - All newly installed cables shall be tested "on the reel" before installation and after final termination. The contractor shall perform Optical Time Domain Reflectometry (OTDR) and Attenuation tests on all fiber strands.
  - Label all new cables and patch panels in accordance with ANSI/TIA-606 and Joint Base Lewis-McChord labeling standards.
  - Provide a detailed communications installation plan and test reports as submittals.

#### 4.0 CONSTRUCTION REQUIREMENTS


- Work Hours: Normal work hours are 0700 to 1600, Monday through Friday, excluding Federal holidays. Exceptions may be authorized with prior approval from the government PM.
- Permits: The Contractor shall obtain all required permits before starting work, including but not limited to digging permits.
- Codes and Specifications: The Contractor shall comply with the most recent editions of all pertinent Local, State, and Federal codes, including the National Electrical Code (NFPA 70), Unified Facilities Criteria (UFC), and applicable installation design standards.
- Environmental: The Contractor shall comply with all environmental regulations, including the submission of an Environmental Protection Plan (EPP) and a Stormwater Pollution Prevention Plan (SWPPP) if applicable.

- Waste Management: The contractor shall create and follow a waste management plan to meet or exceed installation-specific construction and demolition waste diversion goals.
- Utility Outages: Any required utility outages must be coordinated with the government PM a minimum of 14 calendar days in advance.


Project Location – MDC PAC SCIF

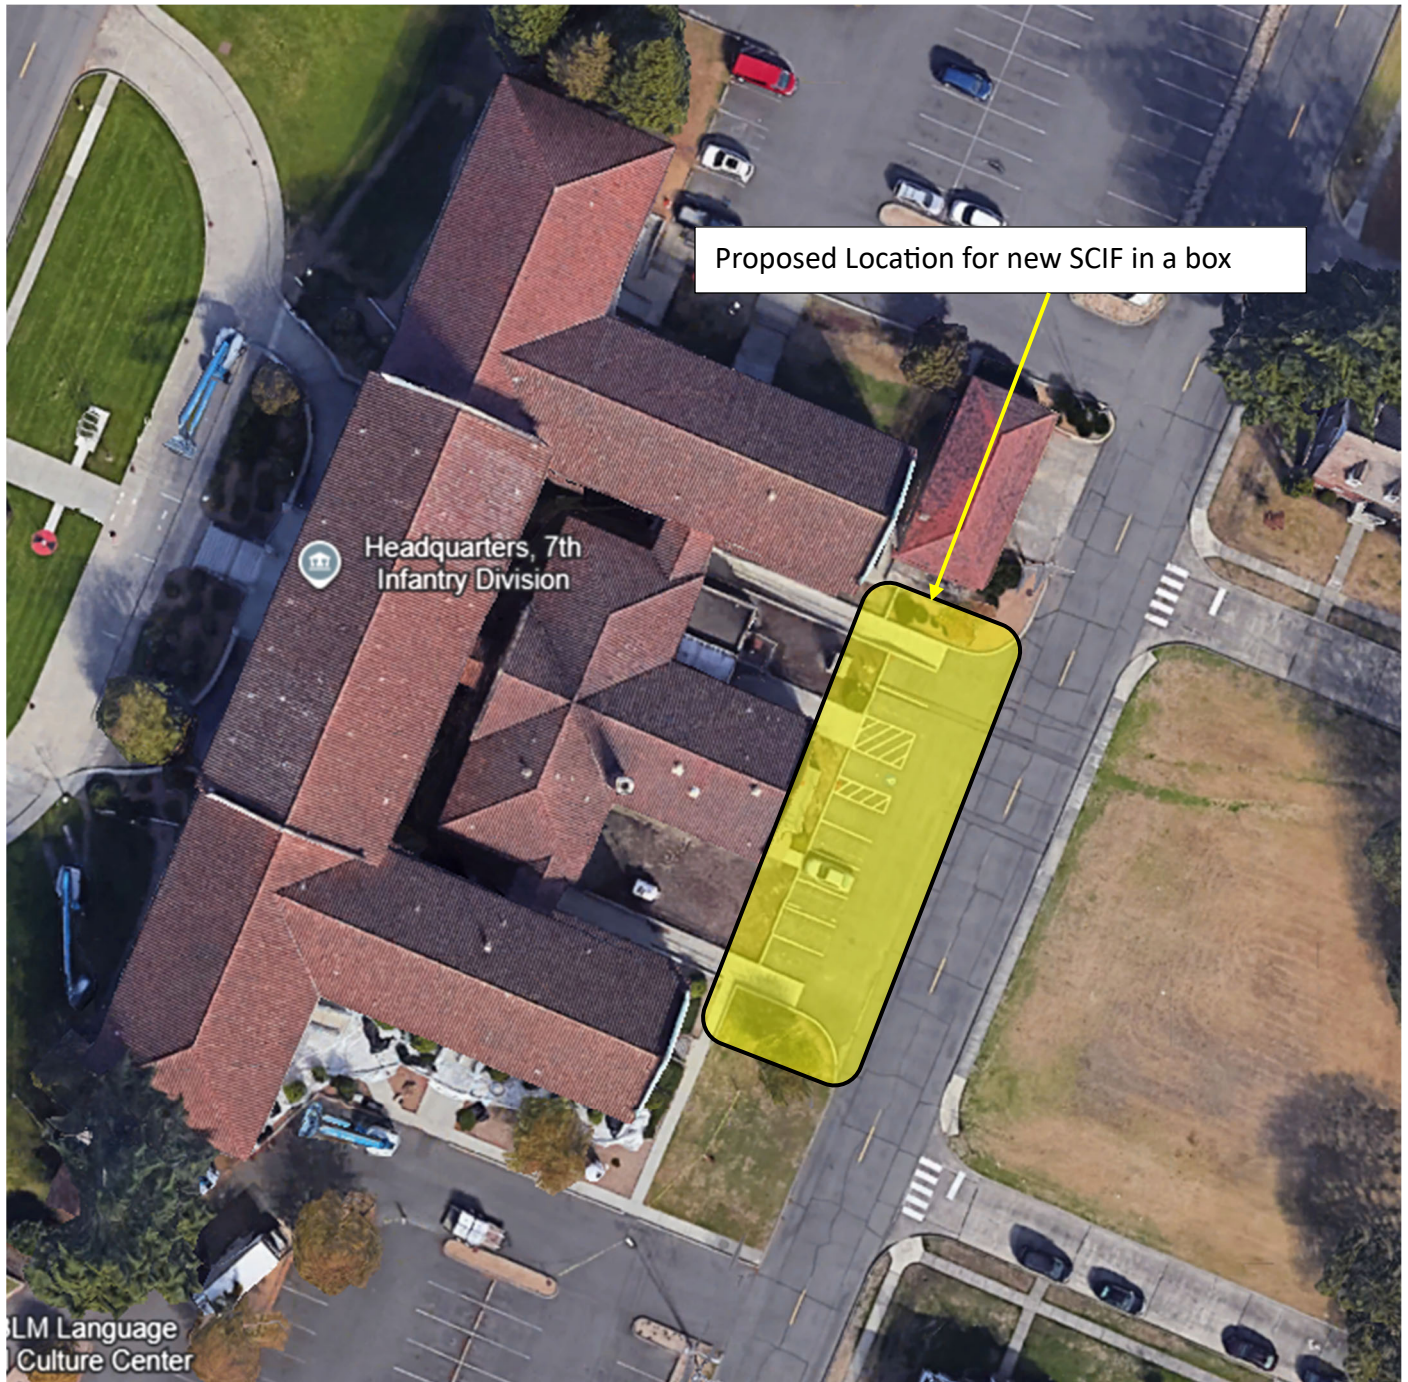

**Example SCIF in a Box Design:**  
\*Contractor must confirm all requirements of scope for final SCIF design.  
\*Contractor not required to use this manufacturer. This is for information only.


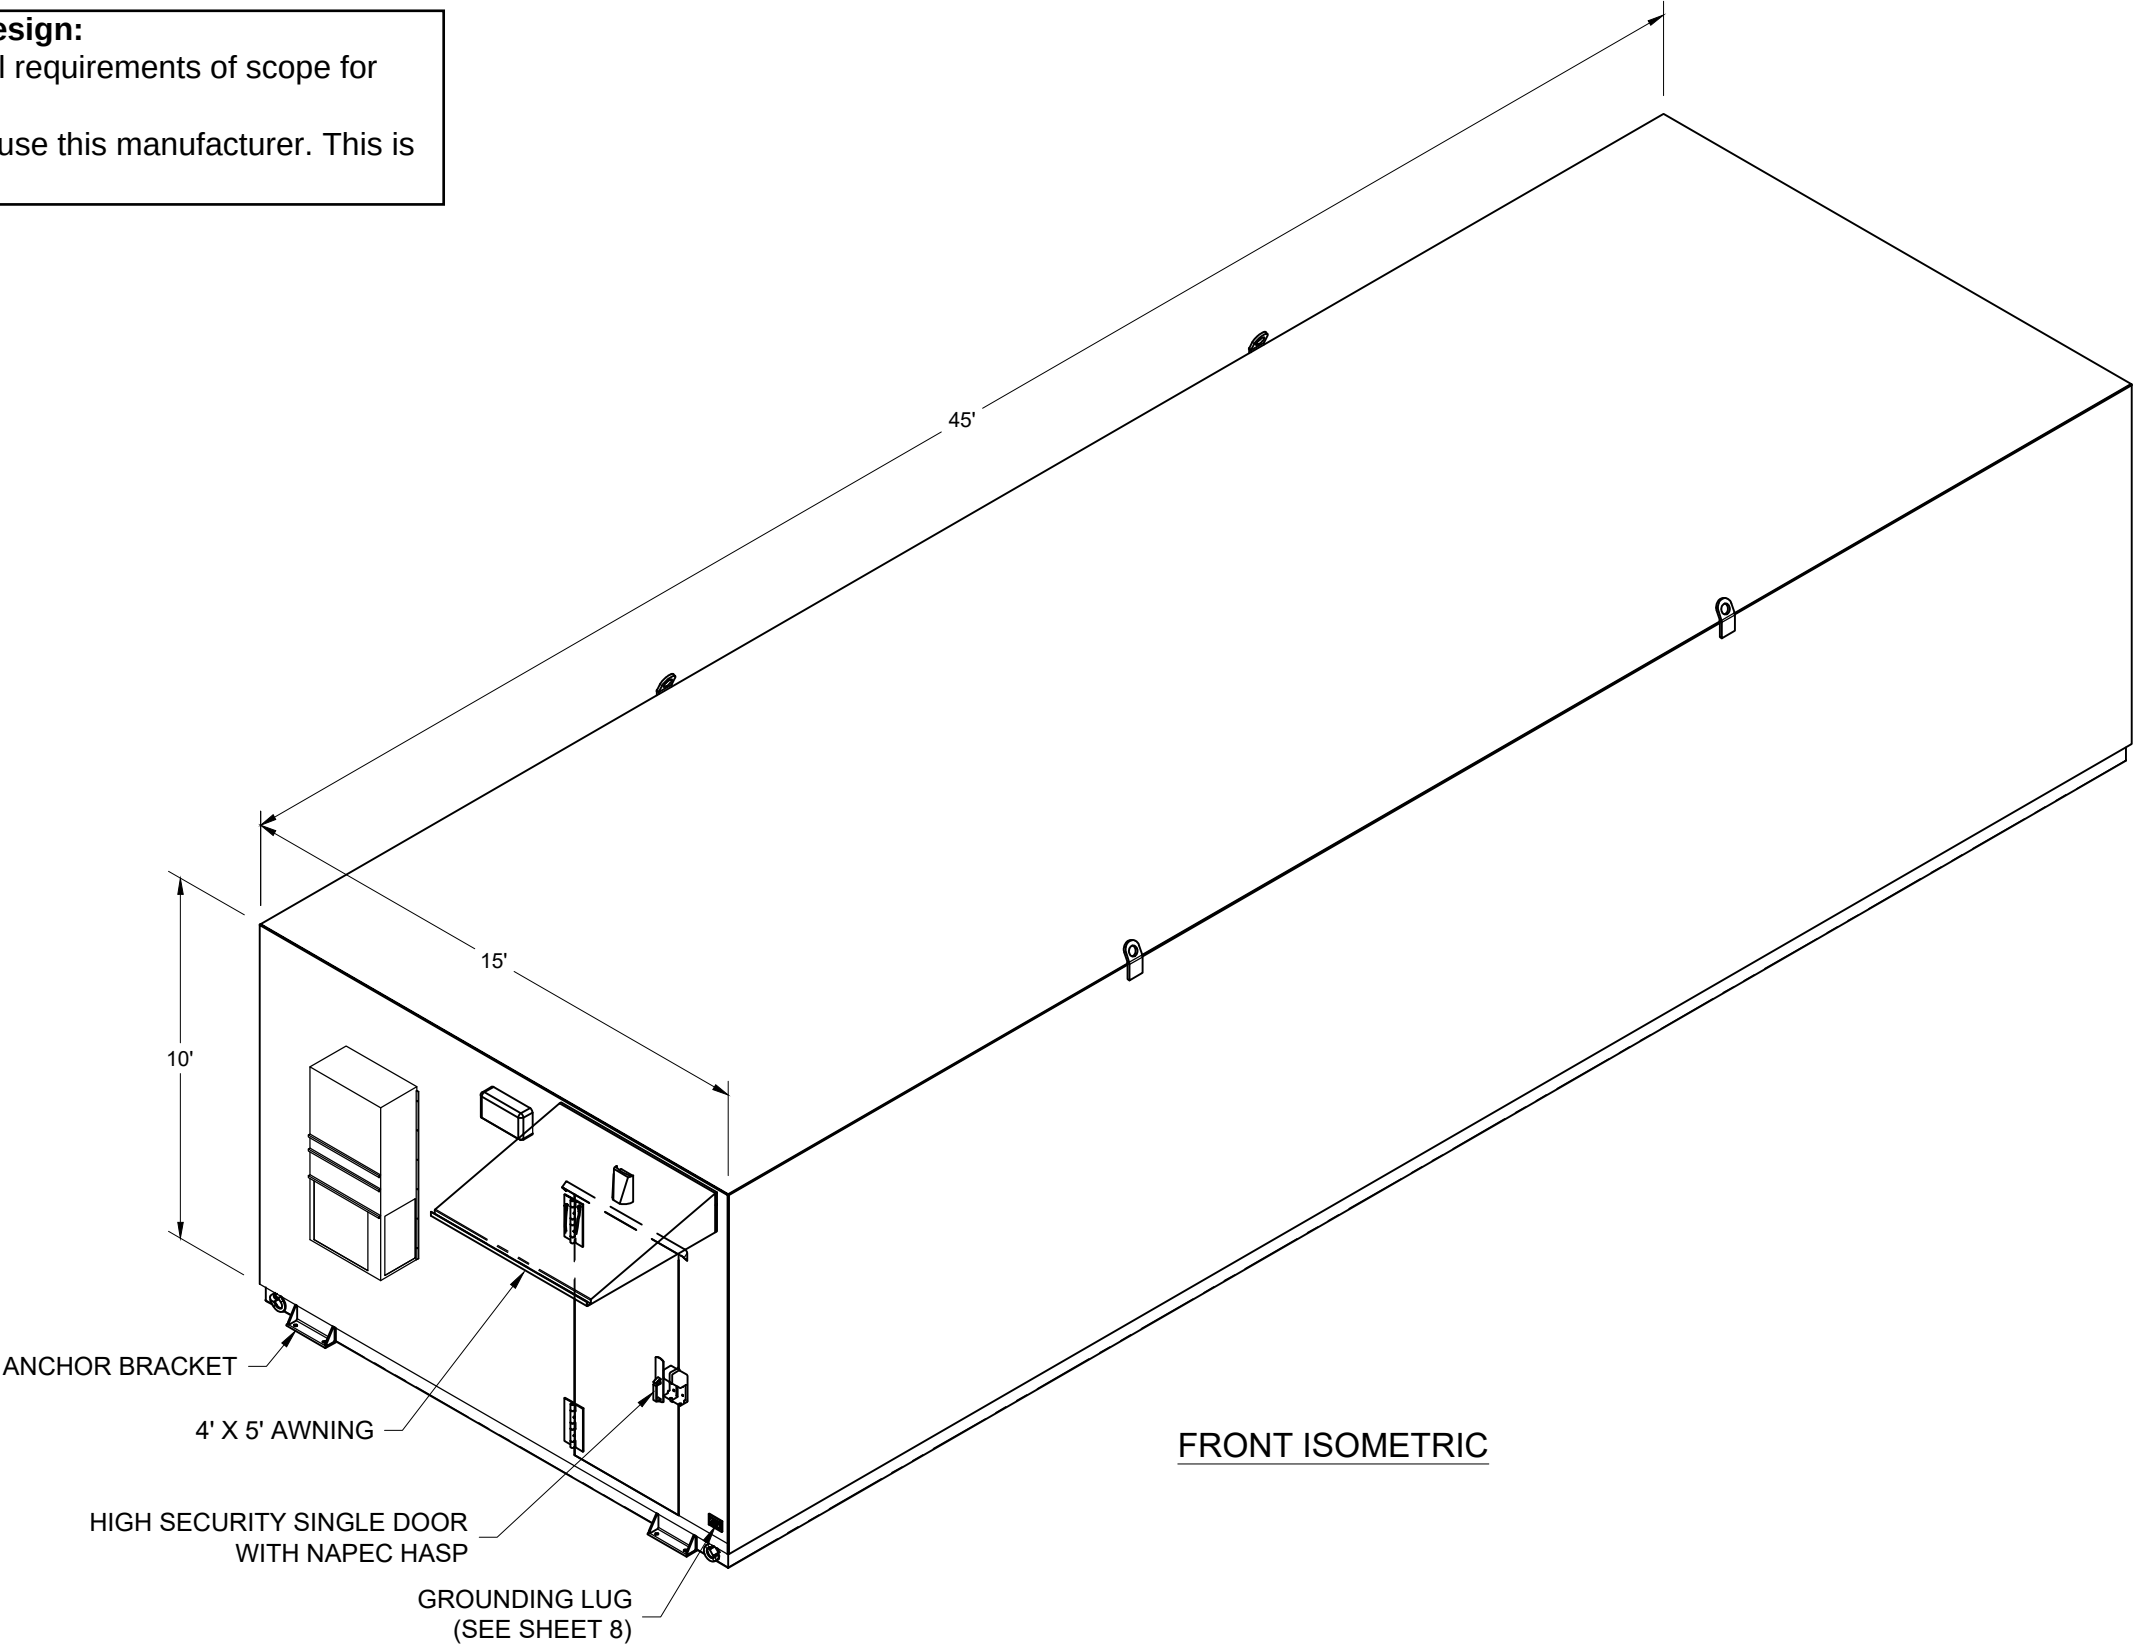


|   |  
|---|--|--------------------------|--|---|--|------------------------|--|------------------------------------------|--|--------------------|--|---|--|---|--|----------------------|--|---------------------------------------|--|----------------|--|
| LEGEND:   |  | LEGEND CONTINUED:        |  | UNLESS OTHERWISE NOTED, TOLERANCES ARE:<br>FRACTIONS: ±1/16" ANGLES: ±1°<br>MACHINED SURFACES: 125 MICRO-INCHES<br>THESE TOLERANCES DO NOT APPLY TO BASIC DIMS.<br>DRAWN TO SCALE UNLESS OTHERWISE NOTED |  | UNIT LENGTH<br>45'     |  | UNIT WIDTH<br>15'                        |  | UNIT HEIGHT<br>10' |  | <div><p><b>ARMAG®</b><br/>C O R P O R A T I O N</p><p>Manufacturers of Arms Vaults and Explosive Storage magazines since 1969<br/>300 ARMAG AVE. • BARDSTOWN, KY 40004 • PHONE: (800) 443-9994 • FAX: (502) 348-4801 • EMAIL: info@armagcorp.com</p></div> |  | DESCRIPTION<br>ARC VAULT WITH RF SHIELDING, DIVIDER WALLS, ALUMINUM AWNING, ACOUSTIC/RF COMBO DOOR, AND NETWORK CABINETS, |  |                      |  | DRAWN BY<br>CTD                       |  | REVISION<br>01 |  |
| ⊙ KILL SWITCH<br>⊖ DURESS<br>⊕ ELECTRIC RECEPTACLE<br>DS DOUBLE STACKED<br>SS SINGLE STACKED<br>EMR EMERGENCY LIGHT<br>T TELEPHONE JACK<br>I LAN CONNECTION<br>SE SEISMIC SENSOR<br>SM SMOKE DETECTION<br>PIR PIR<br>BT BULLET TRAP                                                       |  | ⊕ THERMOSTAT<br>→ GROUND |  | UNIT SPEC<br>ICD 705   |  | UNIT TYPE<br>ARC VAULT |  | DATE DRAWN<br>02/07/2024                 |  | APPROVED BY<br>-   |  |   |  |   |  |                      |  | APPROX. SHIPPING WT. IN LBS<br>80,000 |  |                |  |
| THIS DRAWING IS THE PROPERTY OF ARMAG CORPORATION WHO CLAIMS PROPRIETARY RIGHTS IN THE MATERIAL DISCLOSED. IT IS ISSUED IN CONFIDENCE FOR ENGINEERING INFORMATION ONLY AND MAY NOT BE COPIED OR USED FOR MANUFACTURE OF ANYTHING SHOWN WITHOUT SPECIFIC PERMISSION FROM ARMAG CORPORATION |  |                          |  |   |  | CUSTOMER<br>ADS        |  | LOCATION<br>JOINT BASE LEWIS-MCCHORD, WA |  | SHEET SIZE<br>B    |  |   |  | SCALE<br>1:64   |  | DRAWING NO.<br>S3944 |  |                                       |  |                |  |
|   |  |                          |  |   |  | SERIAL #<br>12070-01   |  | QUOTE #<br>41541                         |  | LINING<br>STC 50   |  |   |  | EXT. FINISH<br>"HAZE GRAY" - DEVTHANE 349QC                                                                               |  | SHEET<br>1 OF 11     |  |                                       |  |                |  |

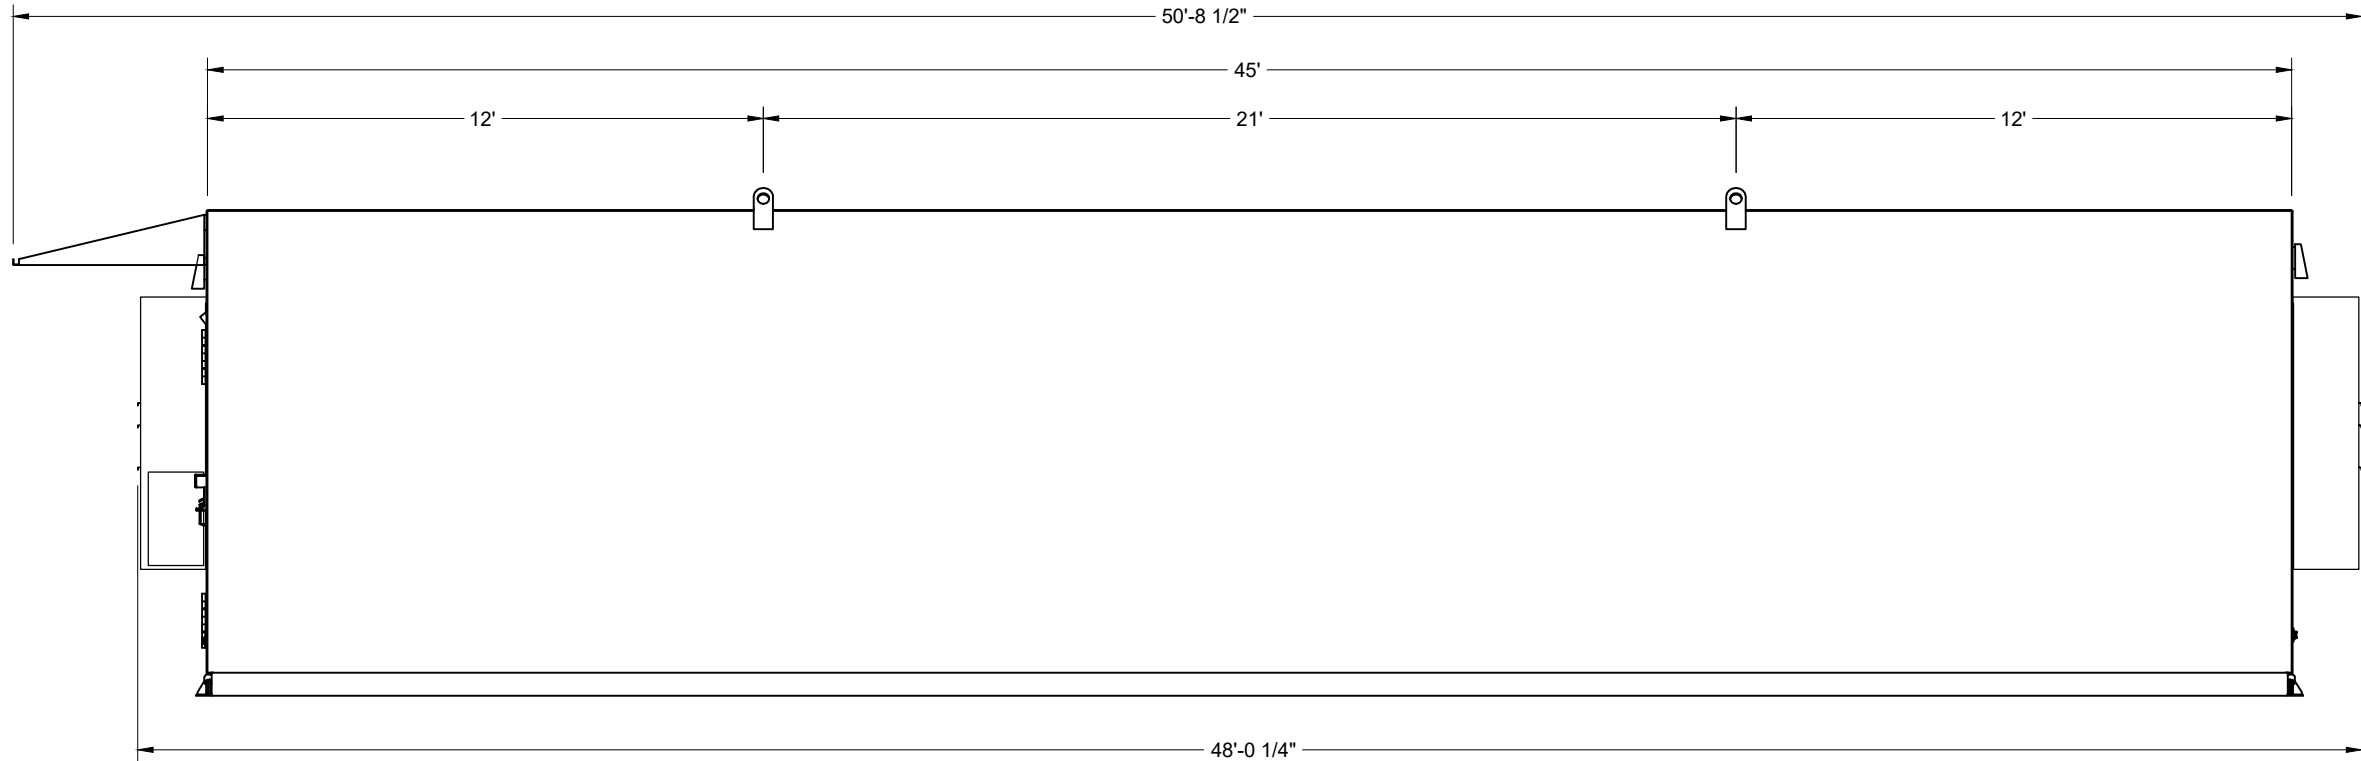


RIGHT SIDE ELEVATION

|         |   |   |   |             |                              |             |   |   |             |                             |
|---------|---|---|---|-------------|------------------------------|-------------|---|---|-------------|-----------------------------|
| LEGEND: | <div><div><div>⊙</div><div>⊕</div><div>⊕</div><div>DS</div><div>SS</div><div>EMR</div><div>Ⓟ</div><div>Ⓜ</div><div>SM</div><div>PIR</div><div>BT</div></div><div><div>KILL SWITCH</div><div>DURESS</div><div>ELECTRIC RECEPTACLE</div><div>DOUBLE STACKED</div><div>SINGLE STACKED</div><div>EMERGENCY LIGHT</div><div>TELEPHONE JACK</div><div>LAN CONNECTION</div><div>SEISMIC SENSOR</div><div>SMOKE DETECTION</div><div>PIR</div><div>BULLET TRAP</div></div></div> | LEGEND CONTINUED: <div><div>⊕</div><div>⊕</div></div> <div><div>THERMOSTAT</div><div>GROUND</div></div> | UNLESS OTHERWISE NOTED, TOLERANCES ARE:<br>FRACTIONS: ±1/16    ANGLES: ±1°<br>MACHINED SURFACES: 125 MICRO-INCHES<br>THESE TOLERANCES DO NOT APPLY TO BASIC DIMS.<br>DRAWN TO SCALE UNLESS OTHERWISE NOTED<br><br>THIS DRAWING IS THE PROPERTY OF ARMAG CORPORATION WHO CLAIMS PROPRIETARY RIGHTS IN THE MATERIAL DISCLOSED. IT IS ISSUED IN CONFIDENCE FOR ENGINEERING INFORMATION ONLY AND MAY NOT BE COPIED OR USED FOR MANUFACTURE OF ANYTHING SHOWN WITHOUT SPECIFIC PERMISSION FROM ARMAG CORPORATION | UNIT LENGTH | UNIT WIDTH                   | UNIT HEIGHT | <div><div><div>ARMAG®</div><div>CORPORATION</div></div><div>Manufacturers of Arms Vaults and Explosive Storage magazines since 1969<br/>300 ARMAG AVE. • BARDSTOWN, KY 40004 • PHONE: (800) 443-9994 • FAX: (502) 348-4801 • EMAIL: info@armagcorp.com</div></div> | DESCRIPTION<br>ARC VAULT WITH RF SHIELDING, DIVIDER WALLS, ALUMINUM AWNING, ACOUSTIC/RF COMBO DOOR, AND NETWORK CABINETS, | DRAWN BY    | REVISION                    |
|         |   |   |   | 45'         | 15'                          | 10'         |   |   | CTD         | 01                          |
|         |   |   |   | UNIT SPEC   | UNIT TYPE                    |             |   |   | DATE DRAWN  |                             |
|         |   |   |   | ICD 705     | ARC VAULT                    |             |   |   | 02/07/2024  |                             |
|         |   |   |   | CUSTOMER    | LOCATION                     |             |   |   | APPROVED BY | APPROX. SHIPPING WT. IN LBS |
|         |   |   |   | ADS         | JOINT BASE LEWIS-MCCHORD, WA |             |   |   | -           |                             |
|         |   |   |   | SHEET       | SERIAL #                     |             |   |   | SHEET SIZE  |                             |
|         |   |   |   | B           | 12070-01                     |             |   |   | B           | 80,000                      |
|         |   |   |   | SCALE       | QUOTE #                      |             |   |   | SCALE       | DRAWING NO.                 |
|         |   |   |   | 1:49.7485   | 41541                        |             |   |   | 1:49.7485   | S3944                       |
| LINING  |   | EXT. FINISH                                                                                             |   | SHEET       |                              |             |   |   |             |                             |
| STC 50  |   | "HAZE GRAY" - DEVTHANE 349QC                                                                            |   | 2 OF 11     |                              |             |   |   |             |                             |

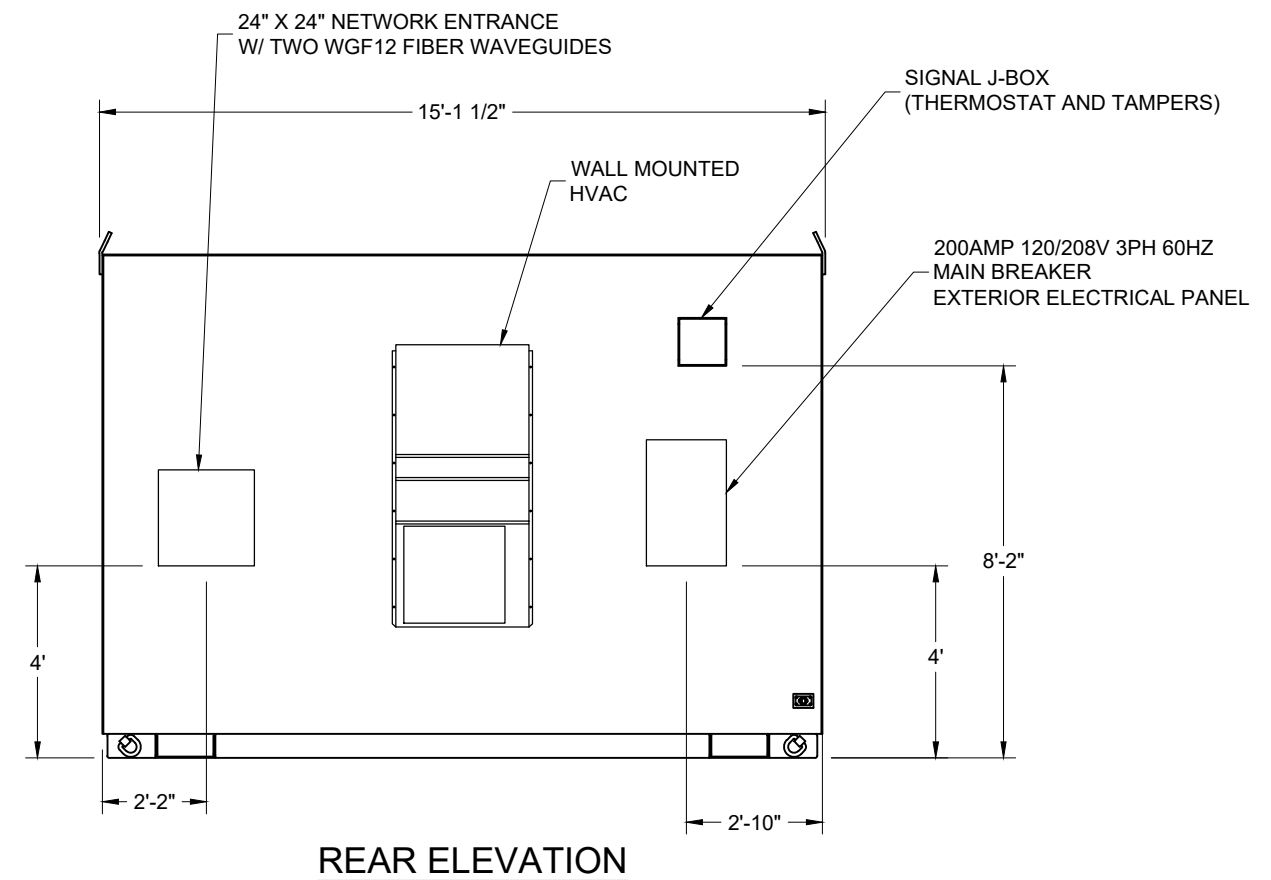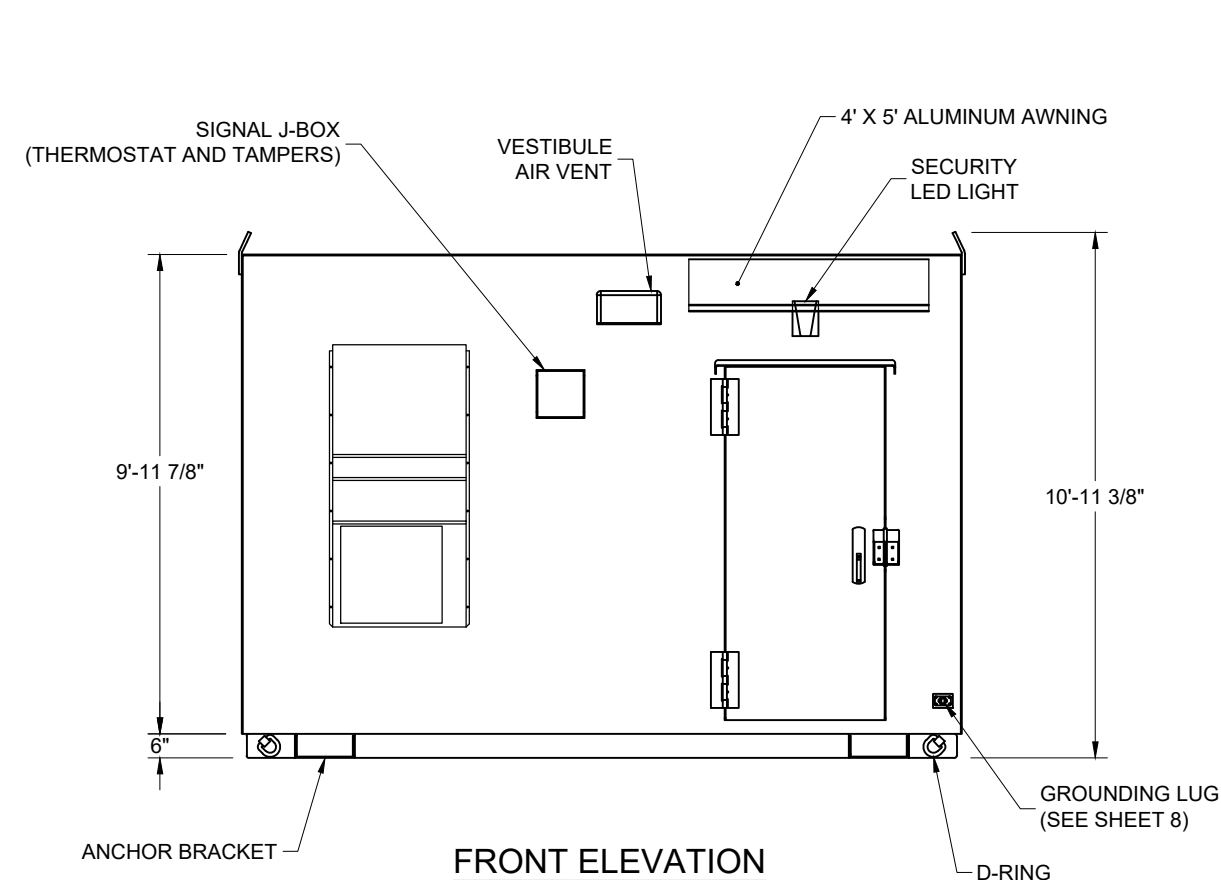


|                     |  
|---------------------|--|-------------------|--|---|--|------------------------|--|-------------------|--|--------------------|--|---|--|---|--|------------------|--|--------------------------|--|---------------------------------------|--|
| LEGEND:             |  | LEGEND CONTINUED: |  | UNLESS OTHERWISE NOTED, TOLERANCES ARE:<br>FRACTIONS: ±1/16 ANGLES: ±1°<br>MACHINED SURFACES: 125 MICRO-INCHES<br>THESE TOLERANCES DO NOT APPLY TO BASIC DIMS<br>DRAWN TO SCALE UNLESS OTHERWISE NOTED<br><br>THIS DRAWING IS THE PROPERTY OF ARMAG CORPORATION WHO CLAIMS PROPRIETARY RIGHTS IN THE MATERIAL DISCLOSED. IT IS ISSUED IN CONFIDENCE FOR ENGINEERING INFORMATION ONLY AND MAY NOT BE COPIED OR USED FOR MANUFACTURE OF ANYTHING SHOWN WITHOUT SPECIFIC PERMISSION FROM ARMAG CORPORATION |  | UNIT LENGTH<br>45'     |  | UNIT WIDTH<br>15' |  | UNIT HEIGHT<br>10' |  | <div>ARMAG®</div> <div>CORPORATION</div> <div>Manufacturers of Arms Vaults and Explosive Storage magazines since 1969</div> <div>300 ARMAG AVE. • BARDSTOWN, KY 40004 • PHONE: (800) 443-9994 • FAX: (502) 348-4801 • EMAIL: info@armagcorp.com</div> |  | DESCRIPTION<br>ARC VAULT WITH RF SHIELDING, DIVIDER WALLS, ALUMINUM AWNING, ACOUSTIC/RF COMBO DOOR, AND NETWORK CABINETS, |  |                  |  | DRAWN BY<br>CTD          |  | REVISION<br>01                        |  |
| ⊙ KILL SWITCH       |  | ⊕ THERMOSTAT      |  |   |  | UNIT SPEC<br>ICD 705   |  |                   |  |                    |  |   |  |   |  |                  |  | DATE DRAWN<br>02/07/2024 |  |                                       |  |
| ⊖ DURESS            |  | ⊥ GROUND          |  |   |  | UNIT TYPE<br>ARC VAULT |  |                   |  |                    |  |   |  |   |  |                  |  | APPROVED BY<br>-         |  | APPROX. SHIPPING WT. IN LBS<br>80,000 |  |
| ⊕ DS DOUBLE STACKED |  |                   |  |   |  | CUSTOMER<br>ADS        |  |                   |  |                    |  |   |  |   |  |                  |  | SHEET SIZE<br>B          |  |                                       |  |
| ⊕ SS SINGLE STACKED |  |                   |  | LOCATION<br>JOINT BASE LEWIS-MCCHORD, WA   |  |                        |  |                   |  |                    |  | LINING<br>STC 50   |  | EXT. FINISH<br>"HAZE GRAY" - DEVTHANE 349QC                                                                               |  | SCALE<br>1:48    |  | DRAWING NO.<br>S3944     |  |                                       |  |
| ⊕ EMERGENCY LIGHT   |  |                   |  |   |  | SERIAL #<br>12070-01   |  | QUOTE #<br>41541  |  |                    |  |   |  |   |  | SHEET<br>3 OF 11 |  |                          |  |                                       |  |
| ⊕ TELEPHONE JACK    |  |                   
| ⊕ LAN CONNECTION    |  |                   
| ⊕ SEISMIC SENSOR    |  |                   
| ⊕ SMOKE DETECTION   |  |                   
| ⊕ PIR               |  |                   
| ⊕ BULLET TRAP       |  |                   

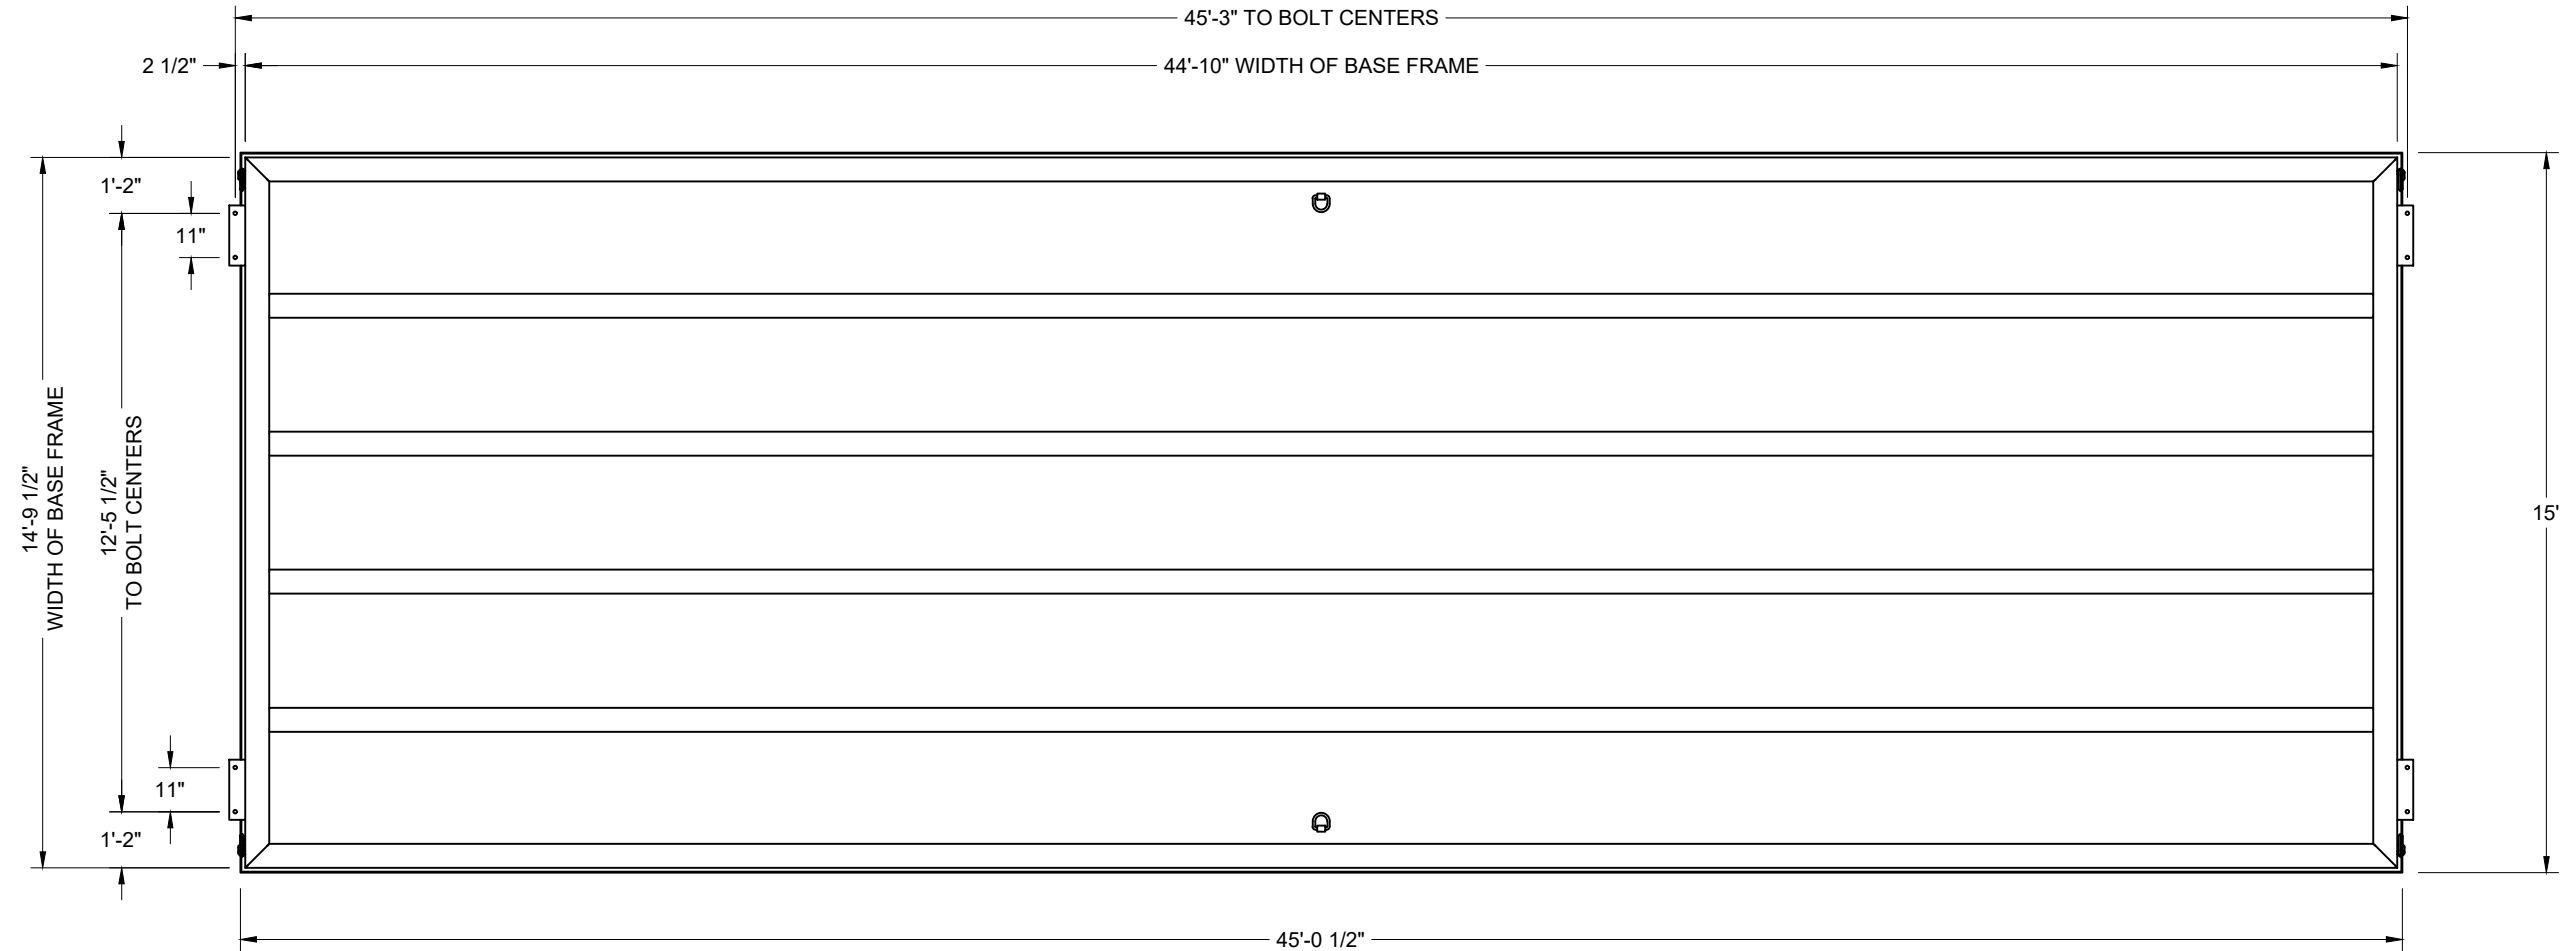

BASE FRAMING PLAN


|   |   |   |                                          |                                       |                    |   |   |                 |                |                  |                                             |                  |  |
|---|---|---|------------------------------------------|---------------------------------------|--------------------|---|---|-----------------|----------------|------------------|---------------------------------------------|------------------|--|
| LEGEND:<br><div><div>⊙</div><div>KILL SWITCH</div></div> <div><div>⊙</div><div>DURESS</div></div> <div><div>⊕</div><div>ELECTRIC RECEPTACLE</div></div> <div><div>DS</div><div>DOUBLE STACKED</div></div> <div><div>SS</div><div>SINGLE STACKED</div></div> <div><div>EMR</div><div>EMERGENCY LIGHT</div></div> <div><div>Ⓣ</div><div>TELEPHONE JACK</div></div> <div><div>LAN</div><div>LAN CONNECTION</div></div> <div><div>SE</div><div>SEISMIC SENSOR</div></div> <div><div>SM</div><div>SMOKE DETECTION</div></div> <div><div>PIR</div><div>PIR</div></div> <div><div>BT</div><div>BULLET TRAP</div></div> | LEGEND CONTINUED:<br><div><div>⊕</div><div>THERMOSTAT</div></div> <div><div>⊕</div><div>GROUND</div></div> | UNLESS OTHERWISE NOTED, TOLERANCES ARE:<br>FRACTIONS: ±1/16    ANGLES: ±1°<br>MACHINED SURFACES: 125 MICRO-INCHES<br>THESE TOLERANCES DO NOT APPLY TO BASIC DIMS.<br>DRAWN TO SCALE UNLESS OTHERWISE NOTED<br><br>THIS DRAWING IS THE PROPERTY OF ARMAG CORPORATION WHO CLAIMS PROPRIETARY RIGHTS IN THE MATERIAL DISCLOSED. IT IS ISSUED IN CONFIDENCE FOR ENGINEERING INFORMATION ONLY AND MAY NOT BE COPIED OR USED FOR MANUFACTURE OF ANYTHING SHOWN WITHOUT SPECIFIC PERMISSION FROM ARMAG CORPORATION | UNIT LENGTH<br>45'                       | UNIT WIDTH<br>15'                     | UNIT HEIGHT<br>10' | <div><b>ARMAG®</b><br/>CORPORATION<br/><small>Manufacturers of Arms Vaults and Explosive Storage magazines since 1969<br/>300 ARMAG AVE. • BARDSTOWN, KY 40004 • PHONE: (800) 443-9994 •<br/>FAX: (502) 348-4801 • EMAIL: info@armagcorp.com</small></div> | DESCRIPTION<br>ARC VAULT WITH RF SHIELDING, DIVIDER WALLS, ALUMINUM AWNING, ACOUSTIC/RF COMBO DOOR, AND NETWORK CABINETS, | DRAWN BY<br>CTD | REVISION<br>01 |                  |                                             |                  |  |
|   |   |   | DATE DRAWN<br>02/07/2024                 |                                       |                    |   |   |                 |                |                  |                                             |                  |  |
|   |   |   | APPROVED BY<br>-                         | APPROX. SHIPPING WT. IN LBS<br>80,000 |                    |   |   |                 |                |                  |                                             |                  |  |
|   |   |   | SHEET SIZE<br>B                          |                                       |                    |   |   |                 |                |                  |                                             |                  |  |
|   |   |   | SCALE<br>1:48                            | DRAWING NO.<br>S3944                  |                    |   |   |                 |                |                  |                                             |                  |  |
|   |   |   | UNIT SPEC<br>ICD 705                     |                                       |                    |   |   |                 |                | LINING<br>STC 50 | EXT. FINISH<br>"HAZE GRAY" - DEVTHANE 349QC | SHEET<br>4 OF 11 |  |
|   |   |   | UNIT TYPE<br>ARC VAULT                   |                                       |                    |   |   |                 |                |                  |                                             |                  |  |
|   |   |   | CUSTOMER<br>ADS                          |                                       |                    |   |   |                 |                |                  |                                             |                  |  |
|   |   |   | LOCATION<br>JOINT BASE LEWIS-MCCHORD, WA |                                       |                    |   |   |                 |                |                  |                                             |                  |  |
|   |   |   | SERIAL #<br>12070-01                     |                                       |                    |   |   |                 |                | QUOTE #<br>41541 |                                             |                  |  |



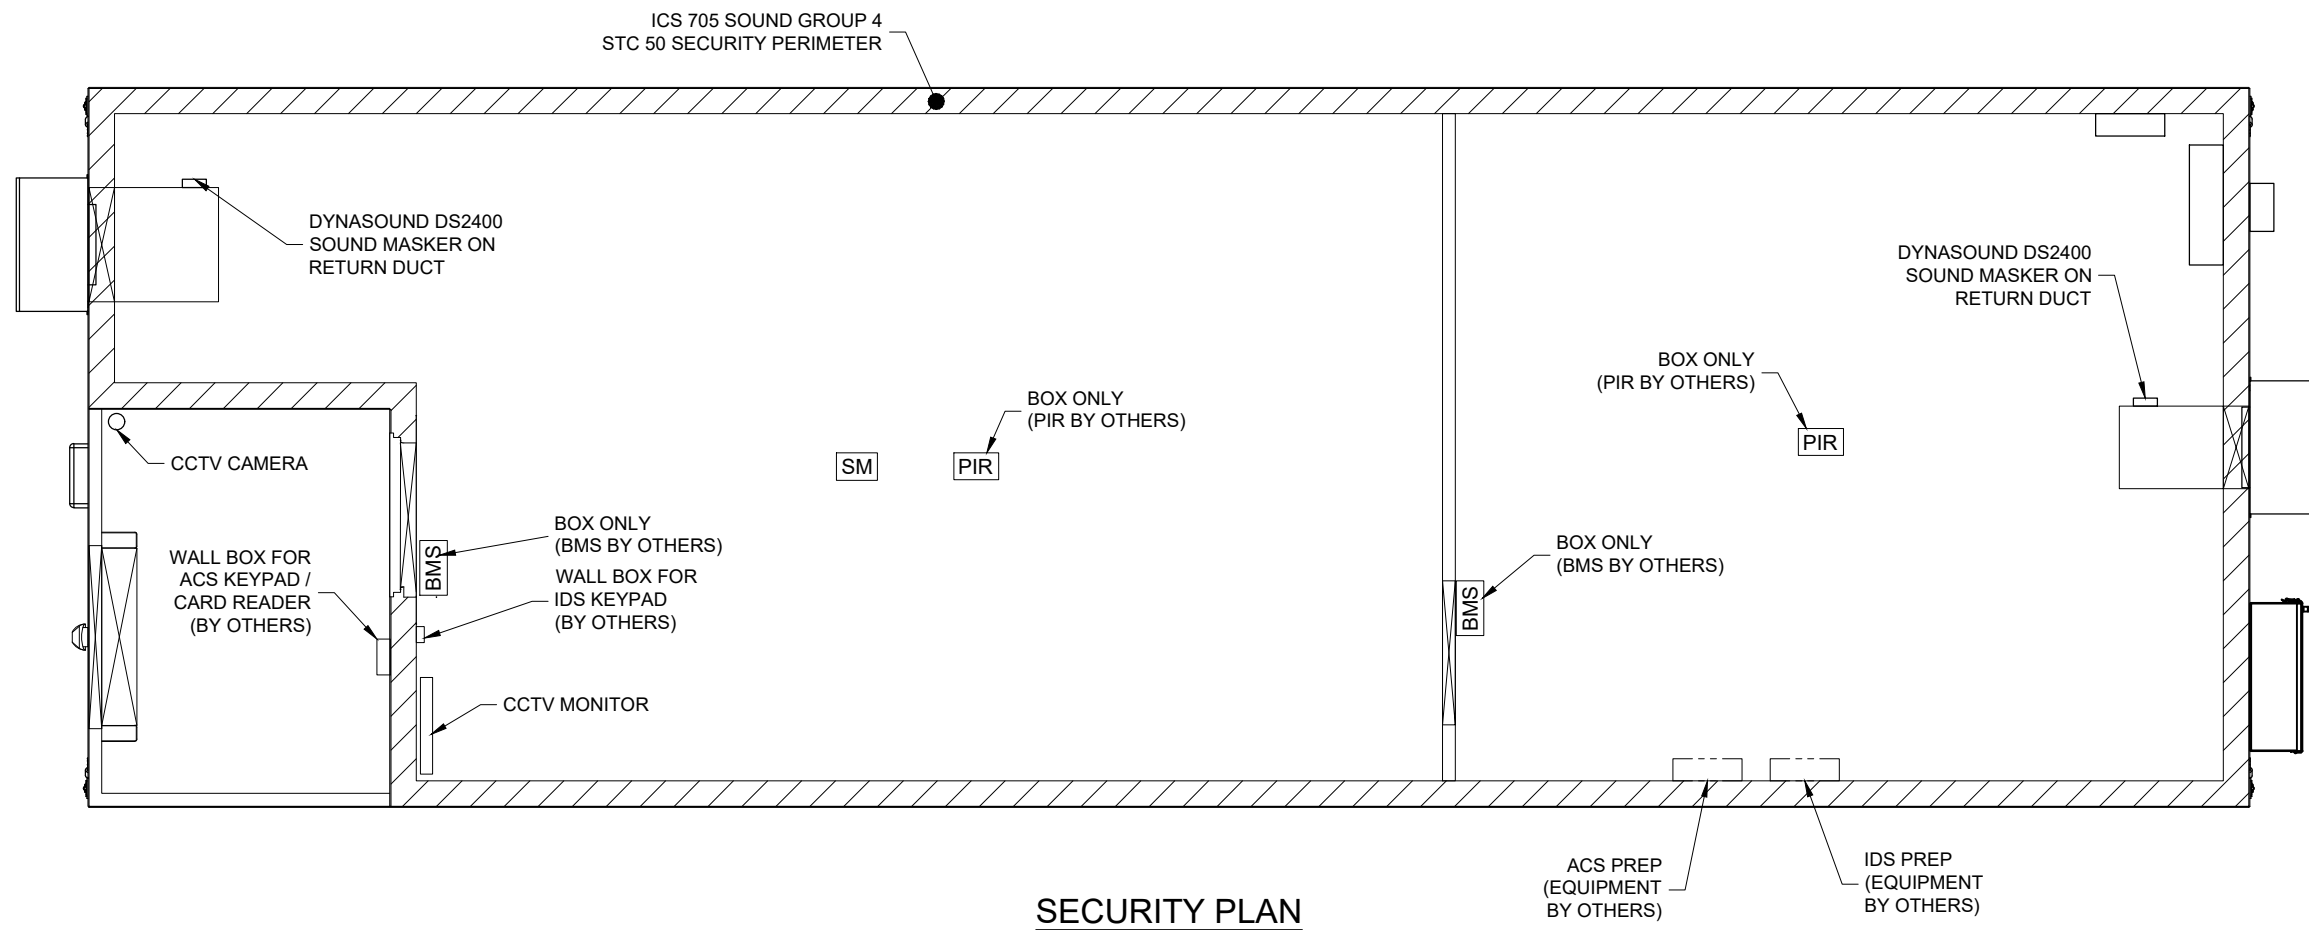

|                       |  |                   |  |   |                          |                                             |                                           |   |   |                 |  |                |
|-----------------------|--|-------------------|--|---|--------------------------|---------------------------------------------|-------------------------------------------|---|---|-----------------|--|----------------|
| LEGEND:               |  | LEGEND CONTINUED: |  | UNLESS OTHERWISE NOTED, TOLERANCES ARE:<br>FRACTIONS: ±1/16 ANGLES: ±1°<br>MACHINED SURFACES: 125 MICRO-INCHES<br>THESE TOLERANCES DO NOT APPLY TO BASIC DIMS.<br>DRAWN TO SCALE UNLESS OTHERWISE NOTED<br><br>THIS DRAWING IS THE PROPERTY OF ARMAG CORPORATION WHO CLAIMS PROPRIETARY RIGHTS IN THE MATERIAL DISCLOSED. IT IS ISSUED IN CONFIDENCE FOR ENGINEERING INFORMATION ONLY AND MAY NOT BE COPIED OR USED FOR MANUFACTURE OF ANYTHING SHOWN WITHOUT SPECIFIC PERMISSION FROM ARMAG CORPORATION | UNIT LENGTH<br>45'       | UNIT WIDTH<br>15'                           | UNIT HEIGHT<br>10'                        | <div><p>ARMAG<sup>®</sup><br/>C O R P O R A T I O N</p><p>Manufacturers of Arms Vaults and Explosive Storage magazines since 1969</p><p>300 ARMAG AVE. • BARDSTOWN, KY 40004 • PHONE: (800) 443-9994 • FAX: (502) 348-4801 • EMAIL: info@armagcorp.com</p></div> | DESCRIPTION<br>ARC VAULT WITH RF SHIELDING, DIVIDER WALLS, ALUMINUM AWNING, ACOUSTIC/RF COMBO DOOR, AND NETWORK CABINETS, | DRAWN BY<br>CTD |  | REVISION<br>01 |
| ⊙ KILL SWITCH         |  | ⊕ THERMOSTAT      |  |   | DATE DRAWN<br>02/07/2024 |                                             | APPROX. SHIPPING WT. IN LBS<br><br>80,000 |   |   |                 |  |                |
| ⊖ DURESS              |  | ⊥ GROUND          |  |   | APPROVED BY              |                                             |                                           |   |   |                 |  |                |
| ⊕ ELECTRIC RECEPTACLE |  |                   |  |   | SHEET SIZE<br>B          |                                             |                                           |   |   |                 |  |                |
| DS DOUBLE STACKED     |  |                   |  |   | SCALE<br>1:48            |                                             | DRAWING NO.<br>S3944                      |   |   |                 |  |                |
| SS SINGLE STACKED     |  |                   |  | SHEET<br>6 OF 11   |                          |                                             |                                           |   |   |                 |  |                |
| EMR EMERGENCY LIGHT   |  |                   |  | LINING<br>STC 50   |                          | EXT. FINISH<br>"HAZE GRAY" - DEVTHANE 349QC |                                           |   |   |                 |  |                |
| Ⓟ TELEPHONE JACK      |  |                   |  | CUSTOMER<br>ADS   |                          |                                             |                                           |   |   |                 |  |                |
| Ⓜ LAN CONNECTION      |  |                   |  | LOCATION<br>JOINT BASE LEWIS-MCCHORD, WA   |                          |                                             |                                           |   |   |                 |  |                |
| SE SEISMIC SENSOR     |  |                   |  | SERIAL #<br>12070-01   |                          | QUOTE #<br>41541                            |                                           |   |   |                 |  |                |
| SM SMOKE DETECTION    |  |                   |  |   |                          |                                             |                                           |   |   |                 |  |                |
| PIR PIR               |  |                   |  |   |                          |                                             |                                           |   |   |                 |  |                |
| BT BULLET TRAP        |  |                   |  |   |                          |                                             |                                           |   |   |                 |  |                |



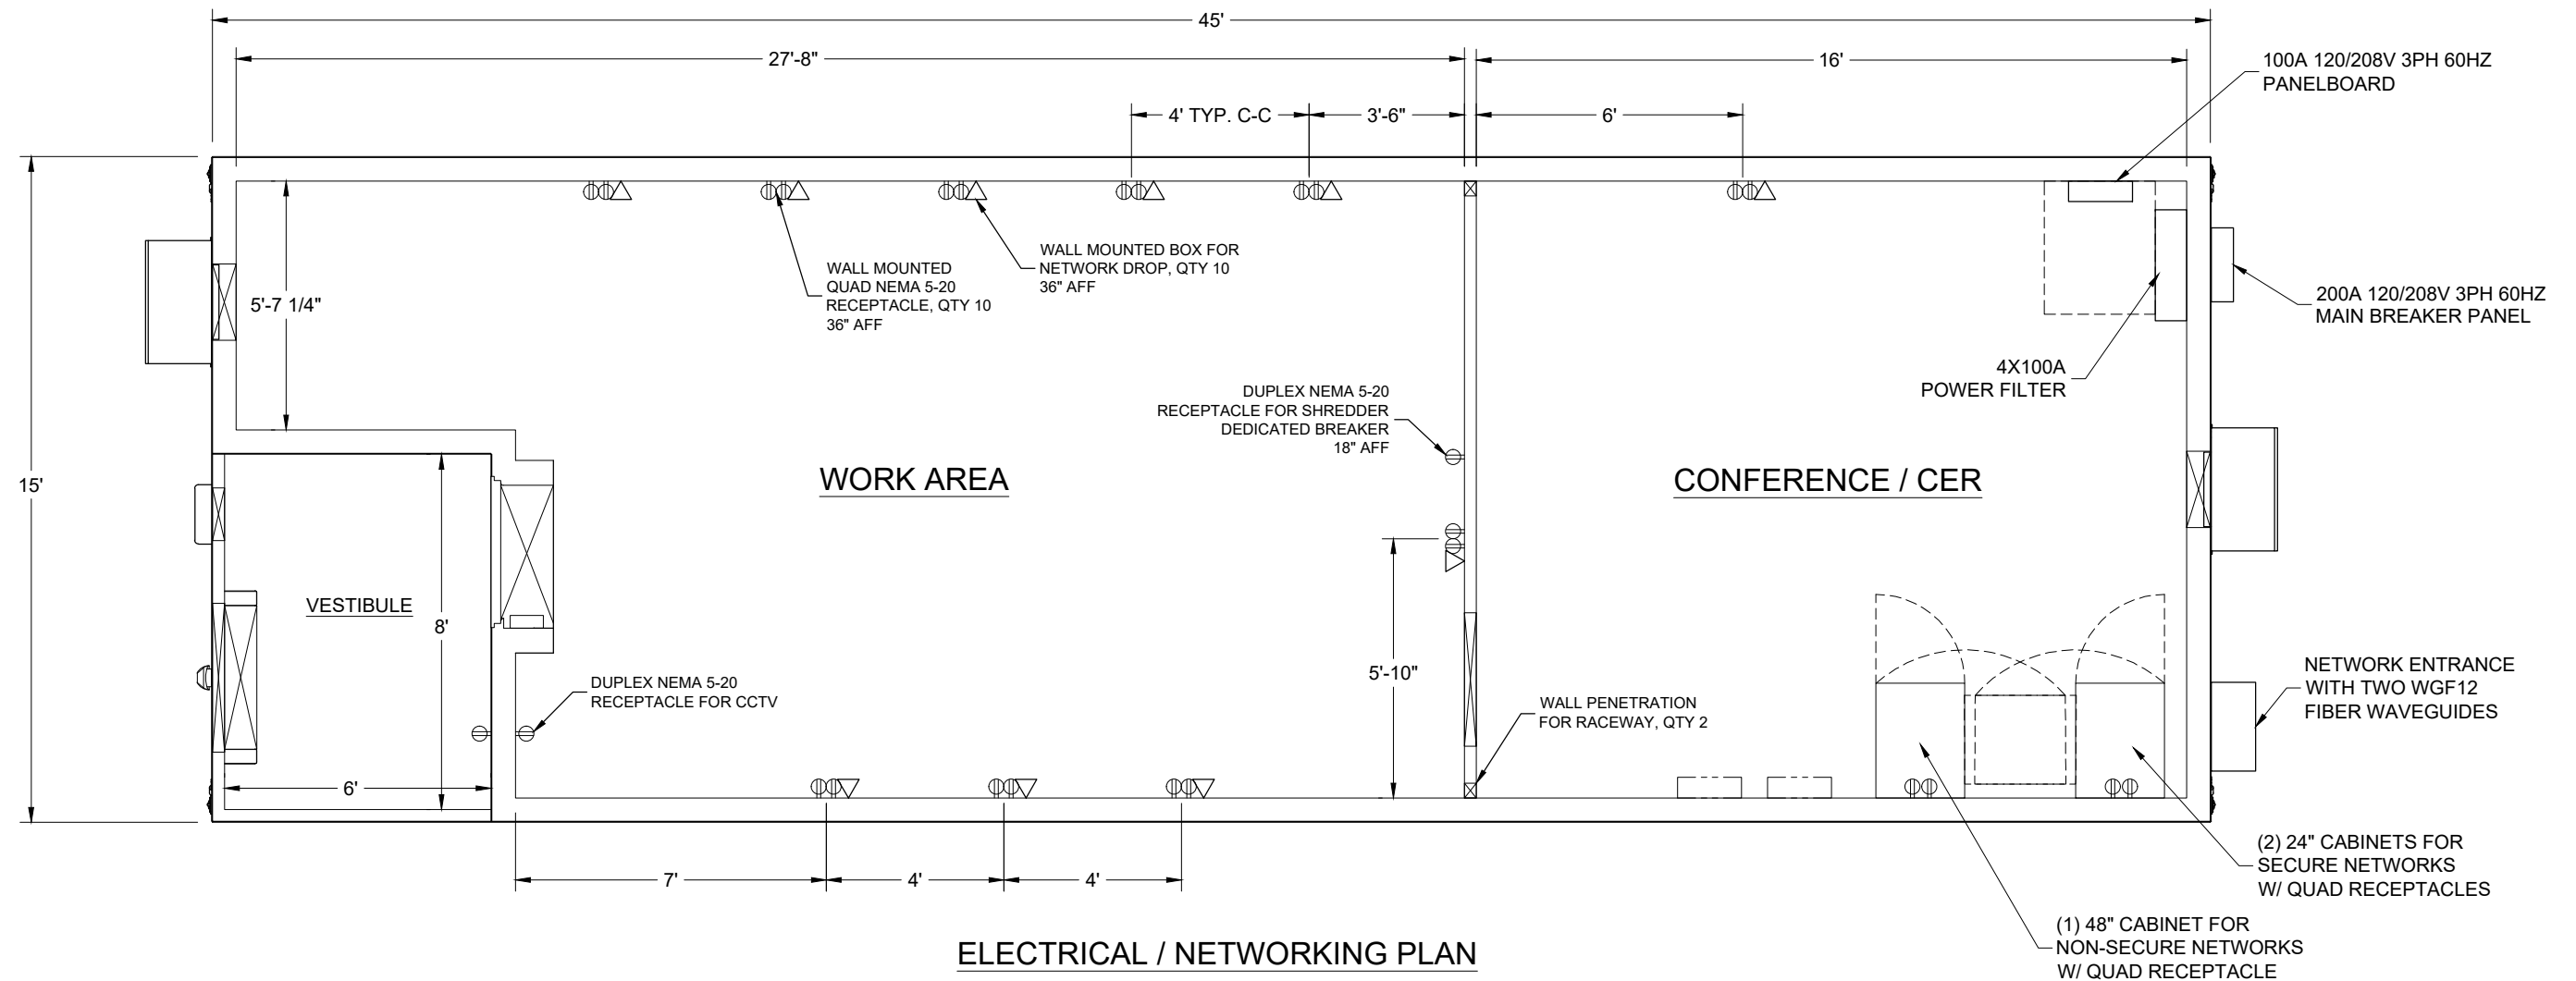


ELECTRICAL / NETWORKING PLAN

|                     |  
|---------------------|--|-------------------|--|---|--|------------------------|--|--------------------------|--|--------------------|--|---|--|---|--|--|--|---------------------------------------|--|----------------|--|
| LEGEND:             |  | LEGEND CONTINUED: |  | UNLESS OTHERWISE NOTED, TOLERANCES ARE:<br>FRACTIONS: ±1/16 ANGLES: ±1°<br>MACHINED SURFACES: 125 MICRO-INCHES<br>THESE TOLERANCES DO NOT APPLY TO BASIC DIMS.<br>DRAWN TO SCALE UNLESS OTHERWISE NOTED<br><br>THIS DRAWING IS THE PROPERTY OF ARMAG CORPORATION WHO CLAIMS PROPRIETARY RIGHTS IN THE MATERIAL DISCLOSED. IT IS ISSUED IN CONFIDENCE FOR ENGINEERING INFORMATION ONLY AND MAY NOT BE COPIED OR USED FOR MANUFACTURE OF ANYTHING SHOWN WITHOUT SPECIFIC PERMISSION FROM ARMAG CORPORATION |  | UNIT LENGTH<br>45'     |  | UNIT WIDTH<br>15'        |  | UNIT HEIGHT<br>10' |  | <div>ARMAG®</div> <div>CORPORATION</div> <div>Manufacturers of Arms Vaults and Explosive Storage magazines since 1969</div> <div>300 ARMAG AVE. • BARDSTOWN, KY 40004 • PHONE: (800) 443-9994 • FAX: (502) 348-4801 • EMAIL: info@armagcorp.com</div> |  | DESCRIPTION<br>ARC VAULT WITH RF SHIELDING, DIVIDER WALLS, ALUMINUM AWNING, ACOUSTIC/RF COMBO DOOR, AND NETWORK CABINETS, |  |  |  | DRAWN BY<br>CTD                       |  | REVISION<br>01 |  |
| ⊗ KILL SWITCH       |  | ⊕ THERMOSTAT      |  |   |  | UNIT SPEC<br>ICD 705   |  | DATE DRAWN<br>02/07/2024 |  | APPROVED BY<br>-   |  |   |  |   |  |  |  | APPROX. SHIPPING WT. IN LBS<br>80,000 |  |                |  |
| ⊙ DURESS            |  | ⊕ GROUND          |  |   |  | UNIT TYPE<br>ARC VAULT |  | SHEET SIZE<br>B          |  | SCALE<br>1:48      |  |   |  |   |  |  |  | DRAWING NO.<br>S3944                  |  |                |  |
| DS DOUBLE STACKED   |  |                   |  |   |  | CUSTOMER<br>ADS        |  | SHEET<br>8 OF 11         |  |                    |  |   |  |   |  |  |  |                                       |  |                |  |
| SS SINGLE STACKED   |  |                   |  | LOCATION<br>JOINT BASE LEWIS-MCCHORD, WA   |  | SERIAL #<br>12070-01   |  | QUOTE #<br>41541         |  | LINING<br>STC 50   |  | EXT. FINISH<br>"HAZE GRAY" - DEVTHANE 349QC   |  |   |  |  |  |                                       |  |                |  |
| EMR EMERGENCY LIGHT |  |                   
| T TELEPHONE JACK    |  |                   
| I LAN CONNECTION    |  |                   
| SE SEISMIC SENSOR   |  |                   
| SM SMOKE DETECTION  |  |                   
| PIR PIR             |  |                   
| BT BULLET TRAP      |  |                   




| EXTERIOR MAIN PANEL SCHEDULE - 120/208V 3Ø RATED PANEL W/ 200A MAIN BREAKER SURFACE MOUNT - NEMA 3R |       |              |                   |             |             |             |                |              |       |      |
|---|-------|--------------|-------------------|-------------|-------------|-------------|----------------|--------------|-------|------|
| BRK.                                                                                                | VOLTS | AMPS / POLES | DESCRIPTION       | LOAD (VA)   |             |             | DESCRIPTION    | AMPS / POLES | VOLTS | BRK. |
|   |       |              |                   | A           | B           | C           |                |              |       |      |
| 1                                                                                                   | 208   | 30/3         | HVAC              | 3600 / 4200 |             |             | HVAC           | 35/3         | 208   | 2    |
| 3                                                                                                   |       |              |                   |             | 3600 / 4200 |             |                |              |       | 4    |
| 5                                                                                                   |       |              |                   |             |             | 3600 / 4200 |                |              |       | 6    |
| 7                                                                                                   | 120   | 20/1         | EXTERIOR LIGHTING | 18 / 230    |             |             | VESTIBULE      | 20/1         | 120   | 8    |
| 9                                                                                                   | 120   | 20/1         | SPARE             |             | - / 3250    |             | INTERIOR POWER | 100/3        | 208   | 10   |
| 11                                                                                                  | 120   | 20/1         | SPARE             |             |             | - / 2400    |                |              |       | 12   |
| 13                                                                                                  | 120   | 20/1         | SPARE             | - / 3140    |             |             |                |              |       | 14   |
| 15                                                                                                  | 120   | 20/1         | SPARE             |             | - / -       |             | SPARE          | 20/1         | 120   | 16   |
| 17                                                                                                  | 120   | 20/1         | SPARE             |             |             | - / -       | SPARE          | 20/1         | 120   | 18   |
| CONNECTED LOAD PER PHASE                                                                            |       |              |                   | 9388        | 11050       | 10200       |                |              |       |      |
| TOTAL CONNECTED LOAD (KVA)                                                                          |       |              |                   | 30.64       |             |             |                |              |       |      |

| INTERIOR SUB PANEL SCHEDULE - 100A 120/208V 3Ø RATED PANEL - MAIN LUG ONLY SURFACE MOUNT - NEMA 1 |       |              |                    |            |            |            |                    |              |       |      |
|---------------------------------------------------------------------------------------------------|-------|--------------|--------------------|------------|------------|------------|--------------------|--------------|-------|------|
| BRK.                                                                                              | VOLTS | AMPS / POLES | DESCRIPTION        | LOAD (VA)  |            |            | DESCRIPTION        | AMPS / POLES | VOLTS | BRK. |
|                                                                                                   |       |              |                    | A          | B          | C          |                    |              |       |      |
| 1                                                                                                 | 120   | 20/1         | NETWORK CABINET #1 | 1000 / 800 |            |            | RECEPTACLES #1-2   | 20/1         | 120   | 2    |
| 3                                                                                                 | 120   | 20/1         | NETWORK CABINET #2 |            | 1000 / 800 |            | RECEPTACLES #3-4   | 20/1         | 120   | 4    |
| 5                                                                                                 | 120   | 20/1         | NETWORK CABINET #3 |            |            | 1000 / 800 | RECEPTACLES #5-6   | 20/1         | 120   | 6    |
| 7                                                                                                 | 120   | 20/1         | CCTV RECEPTACLE    | 180 / 800  |            |            | RECEPTACLES #7-8   | 20/1         | 120   | 8    |
| 9                                                                                                 | 120   | 20/1         | SHREDDER           |            | 400 / 800  |            | RECEPTACLES #9-10  | 20/1         | 120   | 10   |
| 11                                                                                                | 120   | 20/1         | PRINTER            |            |            | 400 / 200  | CER LIGHTING       | 20/1         | 120   | 12   |
| 13                                                                                                | 120   | 20/1         | SPARE              | - / 360    |            |            | IDS / ACS          | 20/1         | 120   | 14   |
| 15                                                                                                | 120   | 20/1         | SPARE              |            | - / 250    |            | WORK AREA LIGHTING | 20/1         | 120   | 16   |
| 17                                                                                                | 120   | 20/1         | SPARE              |            |            | - / -      | SPARE              | 20/1         | 120   | 18   |
| 19                                                                                                | 120   | 20/1         | SPARE              | - / -      |            |            | SPARE              | 20/1         | 120   | 20   |
| 21                                                                                                | 120   | 20/1         | SPARE              |            | - / -      |            | SPARE              | 20/1         | 120   | 22   |
| 23                                                                                                | 120   | 20/1         | SPARE              |            |            | - / -      | SPARE              | 20/1         | 120   | 24   |
| CONNECTED LOAD PER PHASE                                                                          |       |              |                    | 3140       | 3250       | 2400       |                    |              |       |      |
| TOTAL CONNECTED LOAD (KVA)                                                                        |       |              |                    | 8.79       |            |            |                    |              |       |      |

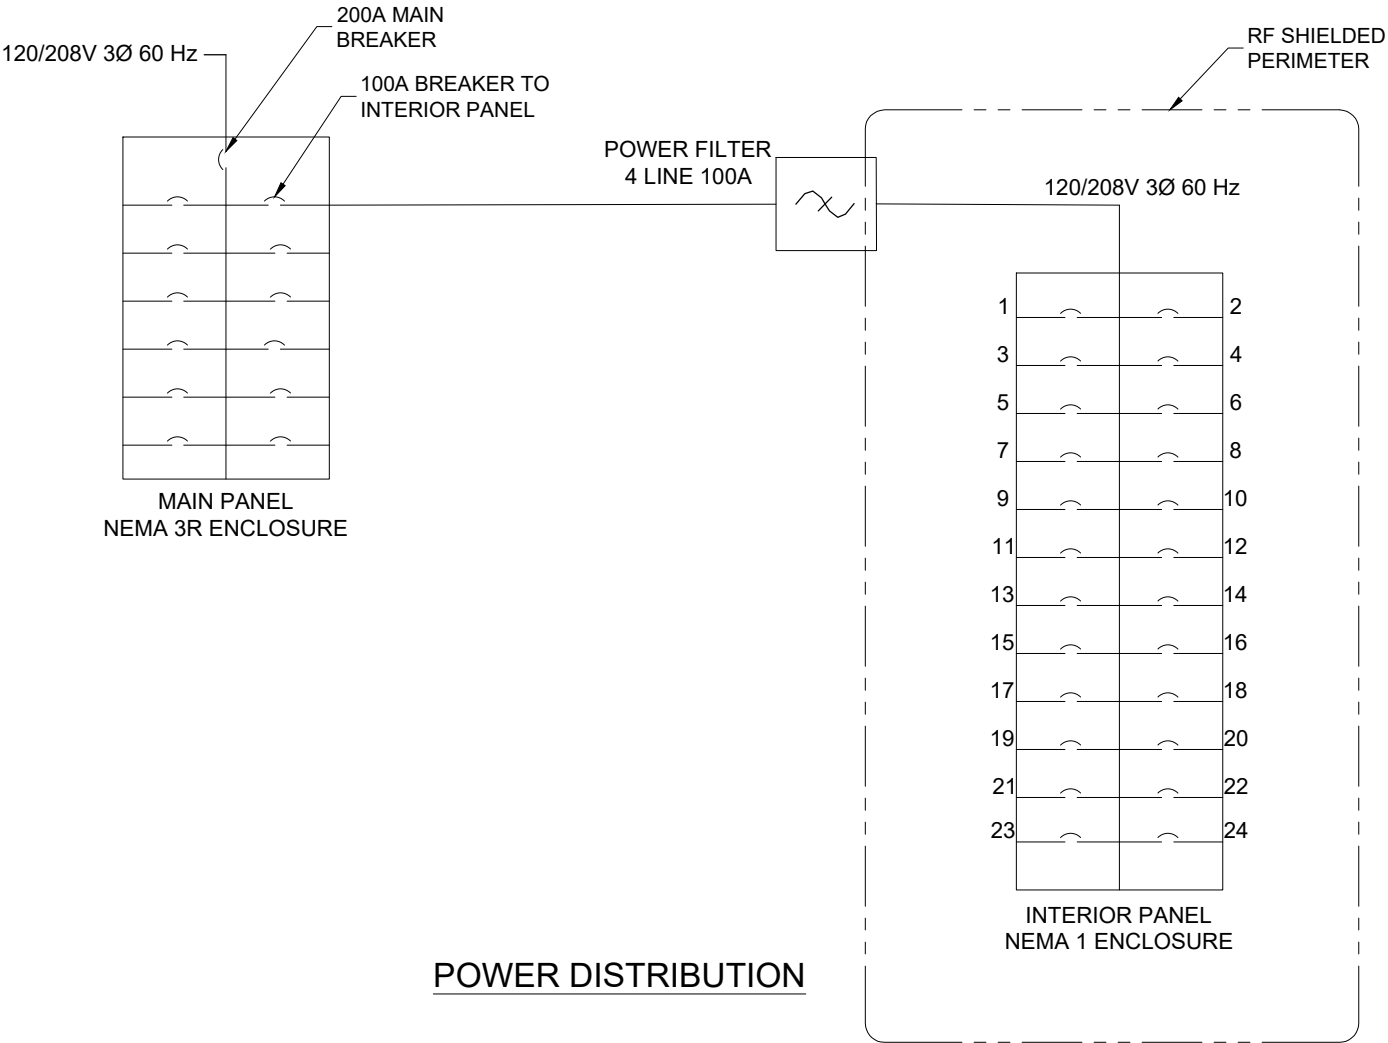


POWER DISTRIBUTION


|   |                                                                                      |   |             |                              |             |   |   |            |          |
|---|--------------------------------------------------------------------------------------|---|-------------|------------------------------|-------------|---|---|------------|----------|
| LEGEND:<br><div><div>⊙</div>KILL SWITCH</div> <div><div>⊙</div>DURESS</div> <div><div>⊕</div>ELECTRIC RECEPTACLE</div> <div><div>DS</div>DOUBLE STACKED</div> <div><div>SS</div>SINGLE STACKED</div> <div><div>EMR</div>EMERGENCY LIGHT</div> <div><div>☎</div>TELEPHONE JACK</div> <div><div>🔌</div>LAN CONNECTION</div> <div><div>📡</div>SEISMIC SENSOR</div> <div><div>🔥</div>SMOKE DETECTION</div> <div><div>👁</div>PIR</div> <div><div>🔫</div>BULLET TRAP</div> | LEGEND CONTINUED:<br><div><div>⊕</div>THERMOSTAT</div> <div><div>⬇</div>GROUND</div> | UNLESS OTHERWISE NOTED, TOLERANCES ARE:<br>FRACTIONS: ±1/16 ANGLES: ±1°<br>MACHINED SURFACES: 125 MICRO-INCHES<br>THESE TOLERANCES DO NOT APPLY TO BASIC DIMS.<br>DRAWN TO SCALE UNLESS OTHERWISE NOTED<br><br>THIS DRAWING IS THE PROPERTY OF ARMAG CORPORATION WHO CLAIMS PROPRIETARY RIGHTS IN THE MATERIAL DISCLOSED. IT IS ISSUED IN CONFIDENCE FOR ENGINEERING INFORMATION ONLY AND MAY NOT BE COPIED OR USED FOR MANUFACTURE OF ANYTHING SHOWN WITHOUT SPECIFIC PERMISSION FROM ARMAG CORPORATION | UNIT LENGTH | UNIT WIDTH                   | UNIT HEIGHT | <div><div>ARMAG®</div><div>CORPORATION</div><div>Manufacturers of Arms Vaults and Explosive Storage magazines since 1969</div><div>300 ARMAG AVE. • BARDSTOWN, KY 40004 • PHONE: (800) 443-9994 • FAX: (502) 348-4801 • EMAIL: info@armagcorp.com</div></div> | DESCRIPTION<br>ARC VAULT WITH RF SHIELDING, DIVIDER WALLS, ALUMINUM AWNING, ACOUSTIC/RF COMBO DOOR, AND NETWORK CABINETS, | DRAWN BY   | REVISION |
|   |                                                                                      |   | 45'         | 15'                          | 10'         |   |   | CTD        | 01       |
|   |                                                                                      |   | UNIT SPEC   | DATE DRAWN                   |             |   |   | 02/07/2024 |          |
|   |                                                                                      |   | ICD 705     | APPROVED BY                  |             |   |   | -          |          |
|   |                                                                                      |   | UNIT TYPE   | SHEET SIZE                   |             |   |   | B          |          |
|   |                                                                                      |   | ARC VAULT   | APPROX. SHIPPING WT. IN LBS  |             |   |   | 80,000     |          |
| CUSTOMER   | LOCATION                                                                             |   | LINING      | EXT. FINISH                  | SCALE       | DRAWING NO.   |   |            |          |
| ADS   | JOINT BASE LEWIS-MCCHORD, WA                                                         |   | STC 50      | "HAZE GRAY" - DEVTHANE 349QC | 1:25.7466   | S3944   |   |            |          |
| SERIAL #   | QUOTE #                                                                              | SHEET   |             |                              |             |   |   |            |          |
| 12070-01   | 41541                                                                                | 10 OF 11   |             |                              |             |   |   |            |          |

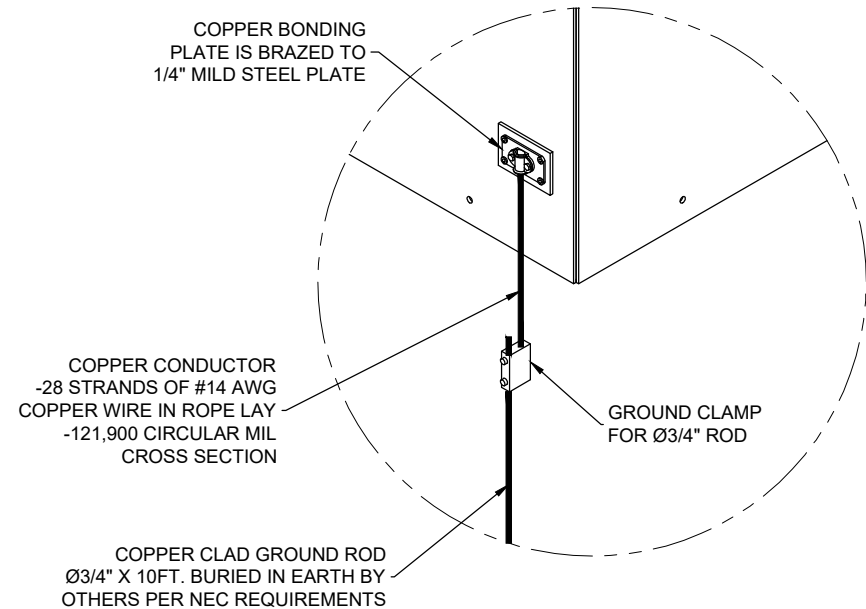

TYPICAL GROUNDING KIT

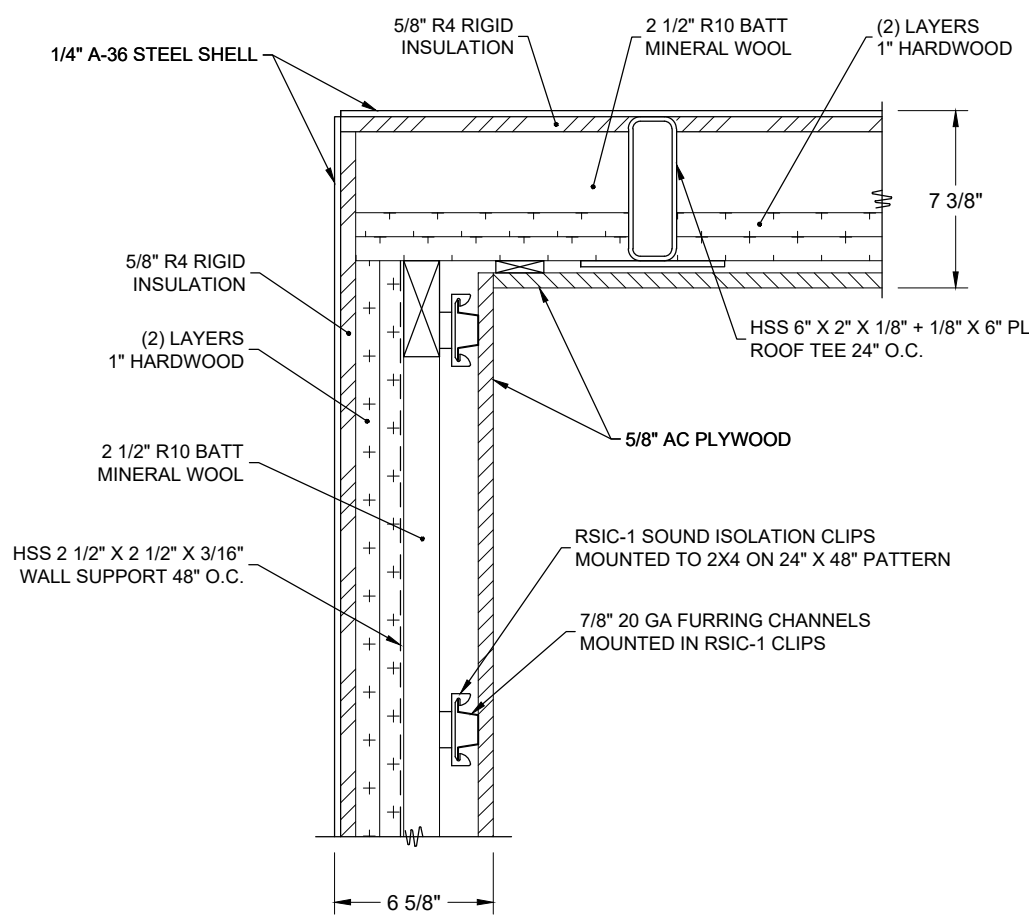

TYPICAL WALL / ROOF CONSTRUCTION

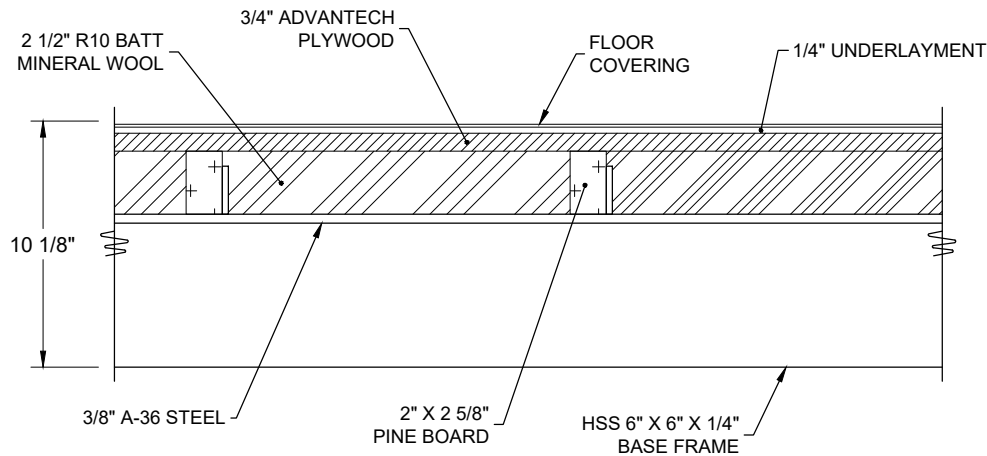

TYPICAL FLOOR CONSTRUCTION

|   |   |   |                                          |                   |                    |   |   |                          |                                       |  |  |
|---|---|---|------------------------------------------|-------------------|--------------------|---|---|--------------------------|---------------------------------------|--|--|
| LEGEND:<br><div><div>⊙</div><div>⊕</div><div>DS</div><div>SS</div><div>EMR</div><div>T</div><div>SE</div><div>SM</div><div>PIR</div><div>BT</div></div> <div><div>KILL SWITCH</div><div>DURESS</div><div>ELECTRIC RECEPTACLE</div><div>DOUBLE STACKED</div><div>SINGLE STACKED</div><div>EMERGENCY LIGHT</div><div>TELEPHONE JACK</div><div>LAN CONNECTION</div><div>SEISMIC SENSOR</div><div>SMOKE DETECTION</div><div>PIR</div><div>BULLET TRAP</div></div> | LEGEND CONTINUED:<br><div><div>⊕</div><div>→</div></div> <div><div>THERMOSTAT</div><div>GROUND</div></div> | UNLESS OTHERWISE NOTED, TOLERANCES ARE:<br>FRACTIONS: ±1/16 ANGLES: ±1°<br>MACHINED SURFACES: 125 MICRO-INCHES<br>THESE TOLERANCES DO NOT APPLY TO BASIC DIMS.<br>DRAWN TO SCALE UNLESS OTHERWISE NOTED<br><br>THIS DRAWING IS THE PROPERTY OF ARMAG CORPORATION WHO CLAIMS PROPRIETARY RIGHTS IN THE MATERIAL DISCLOSED. IT IS ISSUED IN CONFIDENCE FOR ENGINEERING INFORMATION ONLY AND MAY NOT BE COPIED OR USED FOR MANUFACTURE OF ANYTHING SHOWN WITHOUT SPECIFIC PERMISSION FROM ARMAG CORPORATION | UNIT LENGTH<br>45'                       | UNIT WIDTH<br>15' | UNIT HEIGHT<br>10' | <div><div>ARMAG®</div><div>CORPORATION</div><div>Manufacturers of Arms Vaults and Explosive Storage magazines since 1969</div><div>300 ARMAG AVE. • BARDSTOWN, KY 40004 • PHONE: (800) 443-9994 • FAX: (502) 348-4801 • EMAIL: info@armagcorp.com</div></div> | DESCRIPTION<br>ARC VAULT WITH RF SHIELDING, DIVIDER WALLS, ALUMINUM AWNING, ACOUSTIC/RF COMBO DOOR, AND NETWORK CABINETS, | DRAWN BY<br>CTD          | REVISION<br>01                        |  |  |
|   |   |   | UNIT SPEC<br>ICD 705                     |                   |                    |   |   | DATE DRAWN<br>02/07/2024 | APPROX. SHIPPING WT. IN LBS<br>80,000 |  |  |
|   |   |   | UNIT TYPE<br>ARC VAULT                   |                   |                    |   |   | APPROVED BY<br>-         |                                       |  |  |
|   |   |   | CUSTOMER<br>ADS                          |                   |                    |   |   | SHEET SIZE<br>B          |                                       |  |  |
|   |   |   | LOCATION<br>JOINT BASE LEWIS-MCCHORD, WA |                   |                    |   |   | SCALE<br>1:16            | DRAWING NO.<br>S3944                  |  |  |
|   |   |   |                                          |                   |                    |   |   | SERIAL #<br>12070-01     | QUOTE #<br>41541                      |  |  |