








NCO CLUB ——— CAMP GEIGER

MARINE CORPS BASE

CAMP LEJEUNE, N.C.


INDEX OF DRAWINGS

ABBREVIATIONS	NAV. FAC DWG. NO	SHEET NO	TITLE	LEGEND									
AB - ANCHOR BOLT ALU - ALUMINUM BLK - BLOCK CL - CAST IRON CON - CONCRETE CND - CONCRETE VERTICAL JOINT COUL - CONCRETE CONT - CONTINUOUS ELEV - ELEVATION EXT - EXTERIOR FD - FLOOR DRAIN FIN - FINISH FL - FLOOR FR - FLOOR GA - GAUGE GND - GROUND IE - INVERT ELEVATION JH - JOINT MH - MAN HOLE M - MINIMUM M - METAL M - CENTER P - PLATE PND - PIPING RCH - REMOVED CONCRETE PIPE STL - STEEL THK - THICK TYP - TYPICAL WD - WOOD	4011884 4011885 4011886 4011887 4011888 4011889 4011890 4011891 4011892 4011893 4011894 4011895 4011896 4011897 4011898 4011899 4011900 4011901	1 2 3 4 5 6 7 8 9 10 11 12 13 14 15 16 17 18	COVER SHEET AND INDEX; VICINITY MAP SITE PLAN & DETAILS FLOOR PLAN & DETAILS EXTERIOR ELEVATIONS & DRAIN DETAIL SECTIONS & DETAILS INTERIOR ELEVATIONS & SECTIONS BAR ELEVATIONS, SECTIONS & DETAILS DOOR LEGEND & DETAILS REFLECTED CEILING PLAN, FINISH SCHEDULE & SECTIONS FOUNDATION PLAN & SECTIONS ROOF PLAN & SECTIONS HEATING & AIR CONDITIONING PLAN KITCHEN & BAR SCHEDULE W/ INTERIOR ELEVATIONS KITCHEN EQUIPMENT DETAILS PLUMBING PLAN PLUMBING SCHEMATIC ELECTRICAL PLAN, LEGEND, DETAILS & SECTIONS ELECTRICAL PANEL SCHEDULE	2 17 2 17 2 17 DETAIL NUMBER SHEET NUMBER WHERE DETAIL IS TAKEN DETAIL SYMBOL 2 17 2 17 2 17 INTERIOR ELEVATION SYMBOL 2 17 2 17 2 17 SECTION SYMBOL 2 17 2 17 2 17 LETTER INDICATES BUILDING SECTION BUILDING SECTION 2 17 2 17 2 17 DOOR SYMBOL 2 17 2 17 2 17 WINDOW SYMBOL 2 17 2 17 2 17 CONCRETE BLOCK 2 17 2 17 2 17 BRICK 2 17 2 17 2 17 STEEL 2 17 2 17 2 17 WOOD FRAME 2 17 2 17 2 17 FINISH WOOD	SITE LOCATION VICINITY MAP SCALE 1" = 600'-0"								
SATISFACTORY TO DATE 3/24/76					REVISIONS <table><tr><th>SYM</th><th>DESCRIPTION</th><th>DATE</th><th>APPROVED</th></tr><tr><td> </td><td> </td><td> </td><td> </td></tr></table> PUBLIC WORKS DEPT. MARINE CORPS BASE CAMP LEJEUNE, N.C. DEPARTMENT OF THE NAVY NAVAL FACILITIES ENGINEERING COMMAND ATLANTIC DIVISION MARINE CORPS BASE, CAMP LEJEUNE, N.C. DESIGNED BY PROJ MGR APPROVED PUBLIC WORKS OFFICER SATSFACTORY TO DR CHK DATE DATE DATE NCO CLUB, CAMP GEIGER MARINE CORPS BASE, CAMP LEJEUNE, N.C. COVER SHEET & INDEX; VICINITY MAP COMMANDING GENERAL EFD NO APPROVED FOR COMMANDER, NAVFAC RVD DIR DATE SIZE F CODE IDENT NO 80091 NAVFAC DRAWING NO 4011884 CONSTR CONTR NO N62470-75-B-0919 SCALE GRAPHIC SPEC O5-75-0919 SHEET 1 OF 18	SYM	DESCRIPTION	DATE	APPROVED				
SYM	DESCRIPTION	DATE	APPROVED										

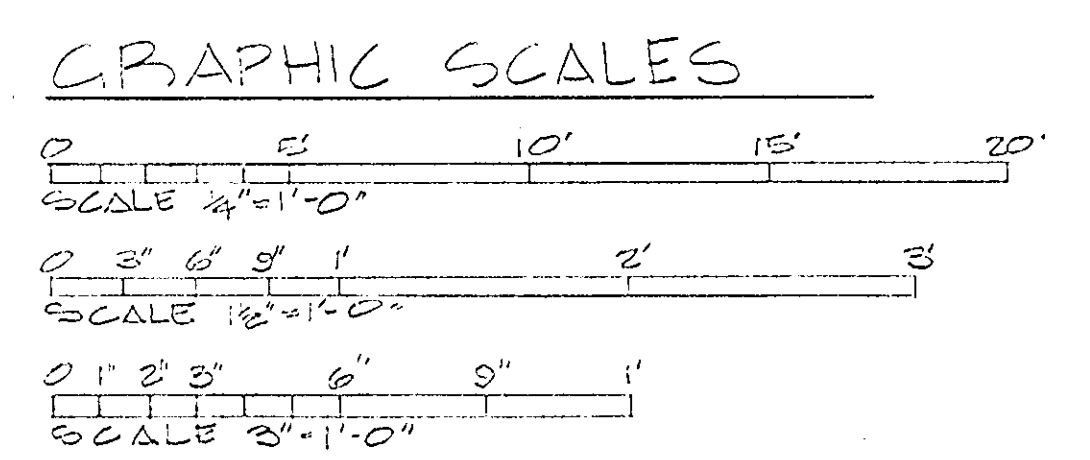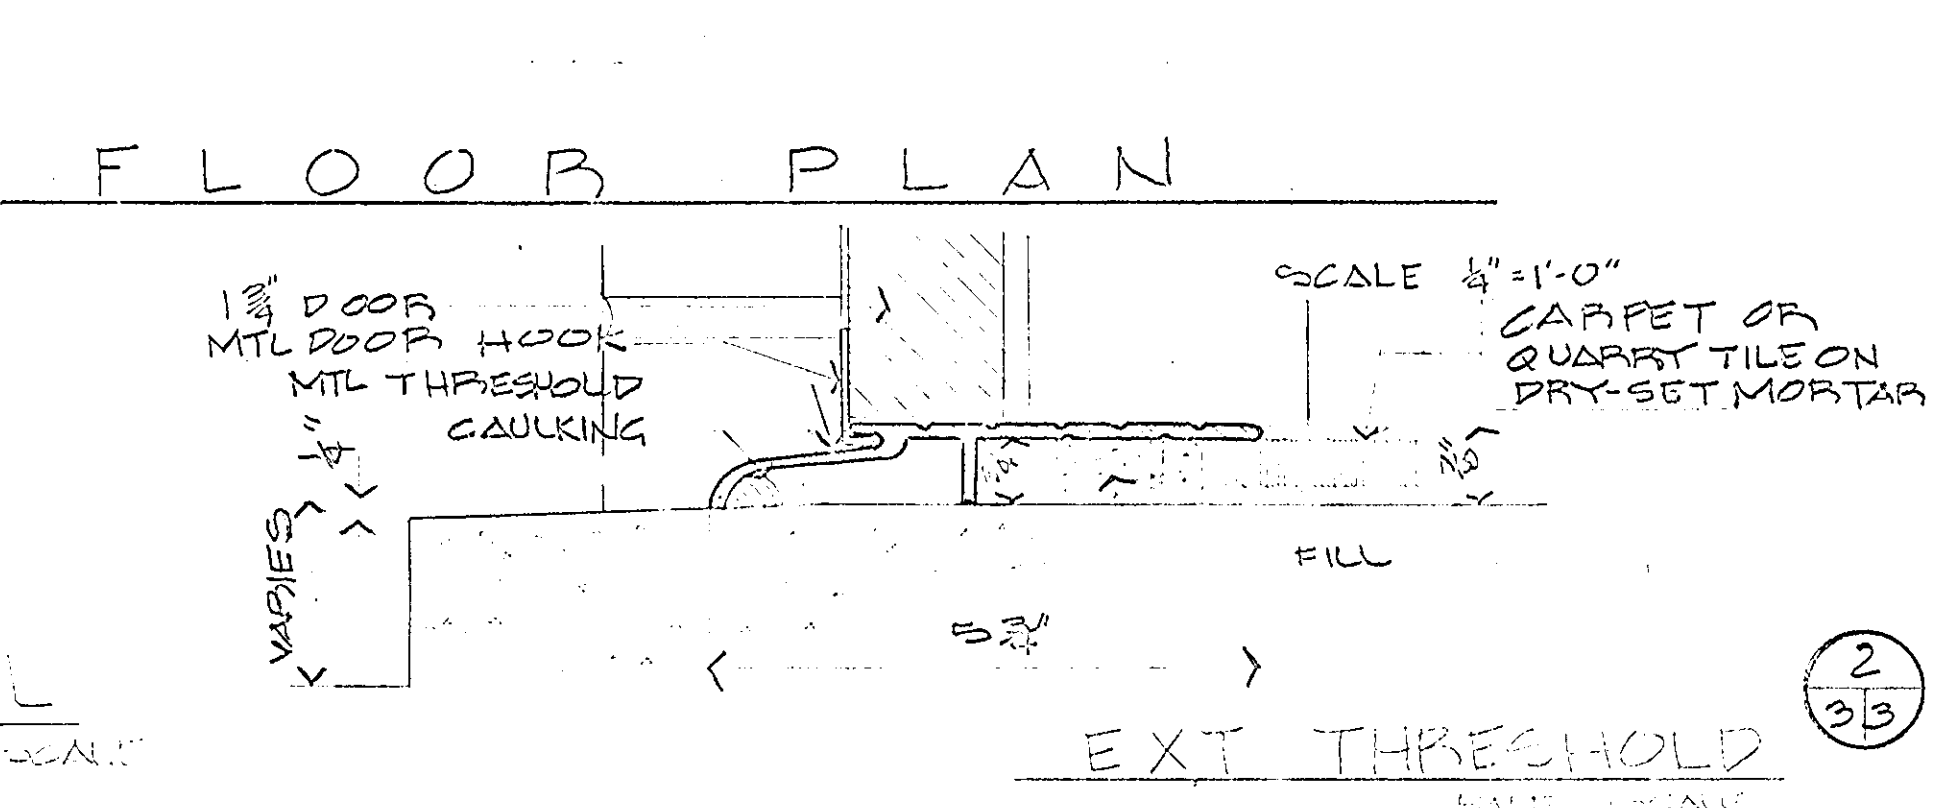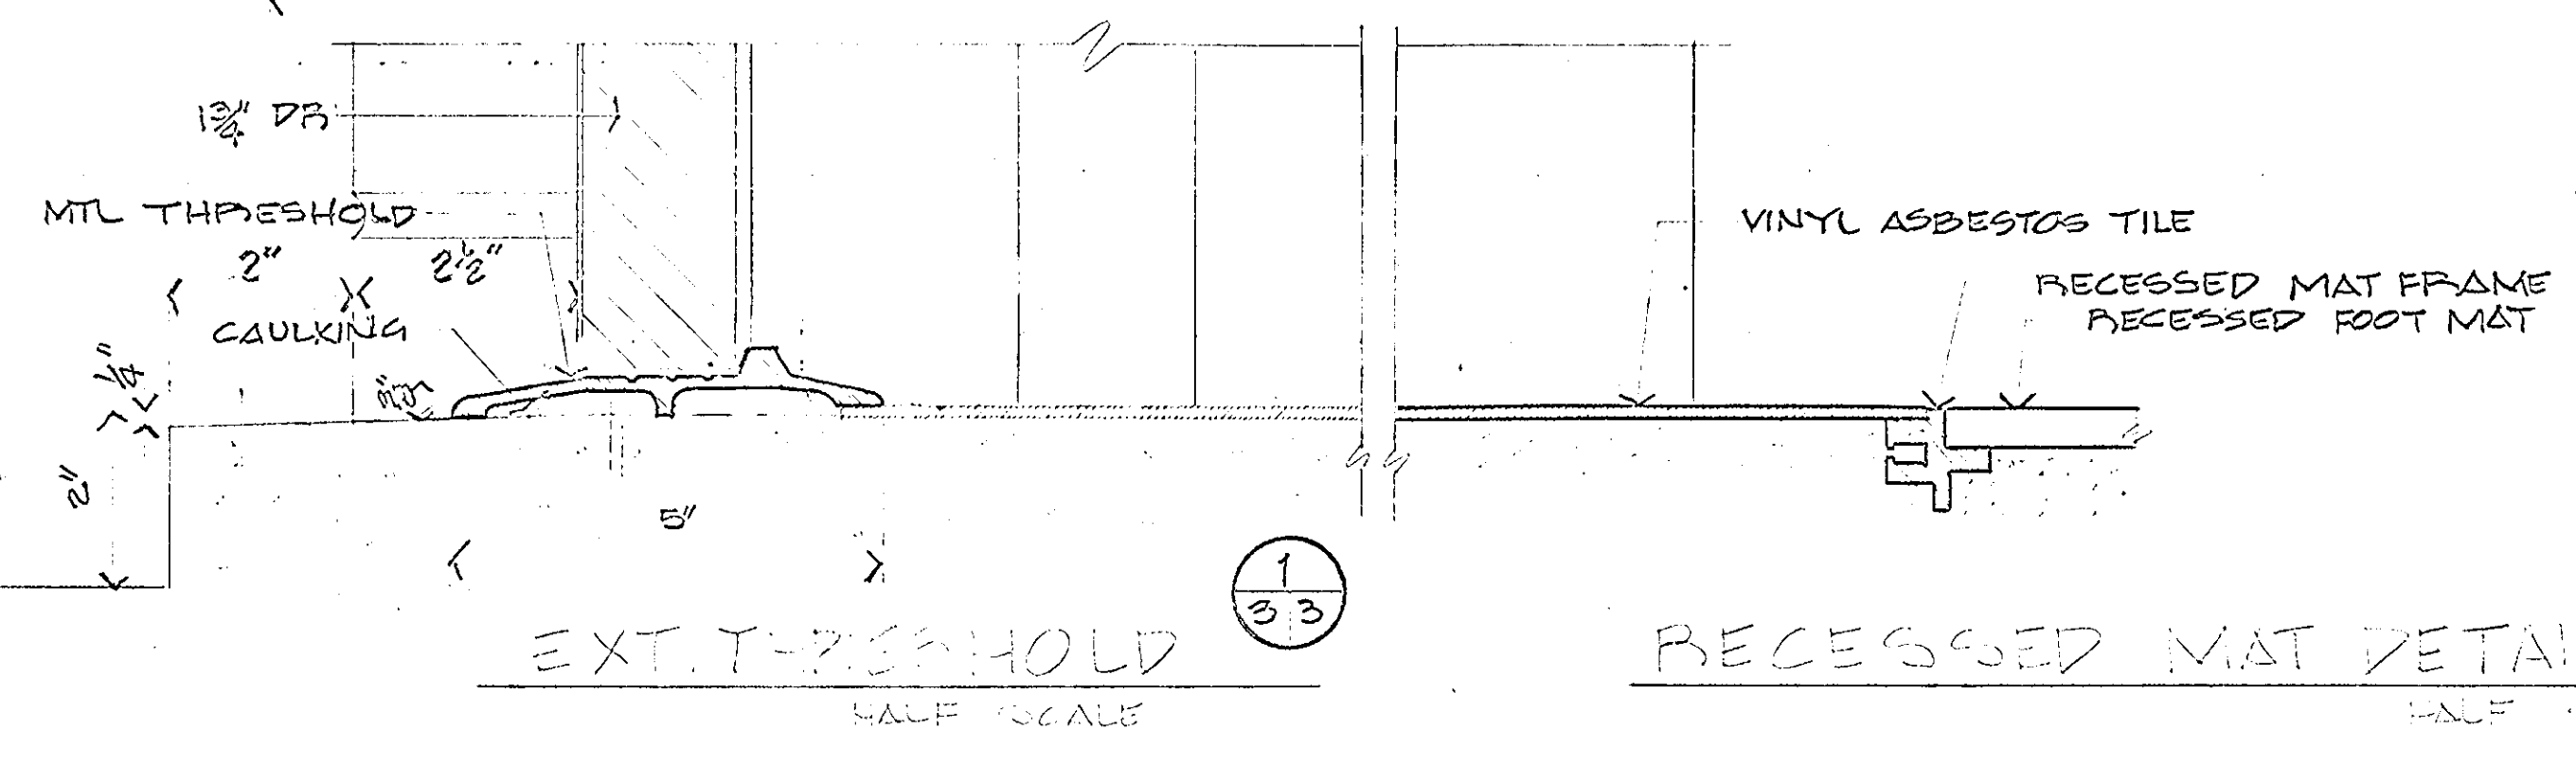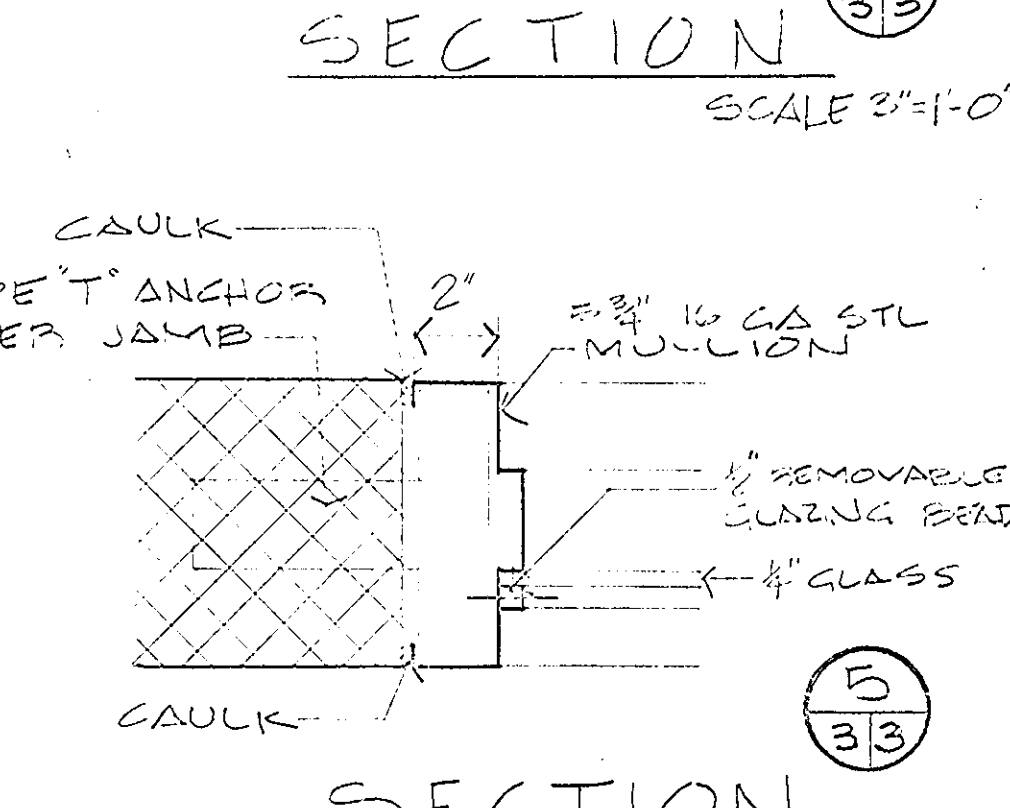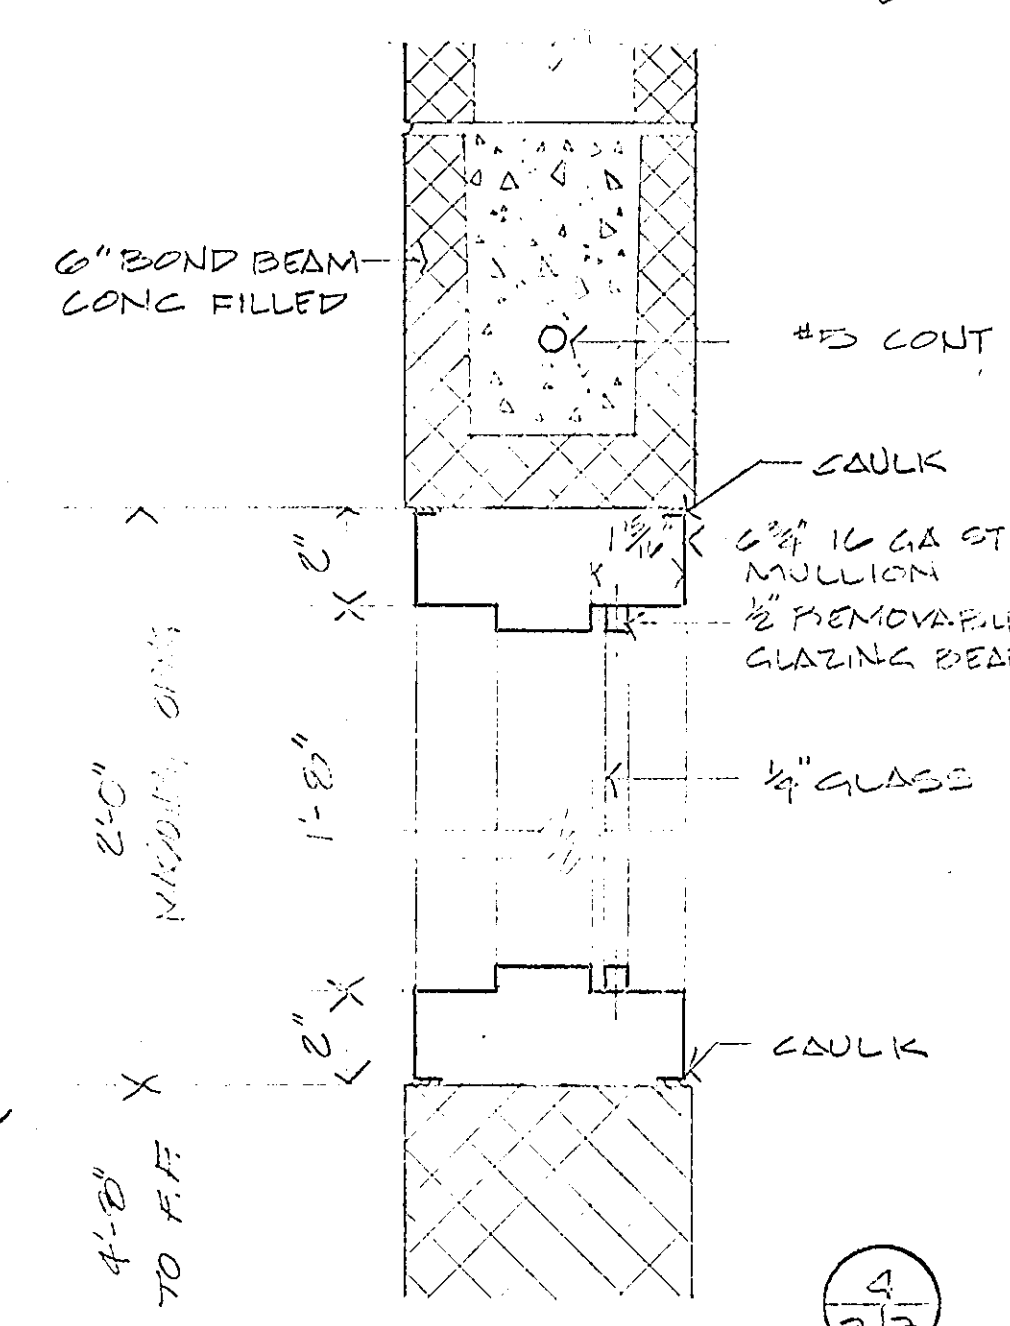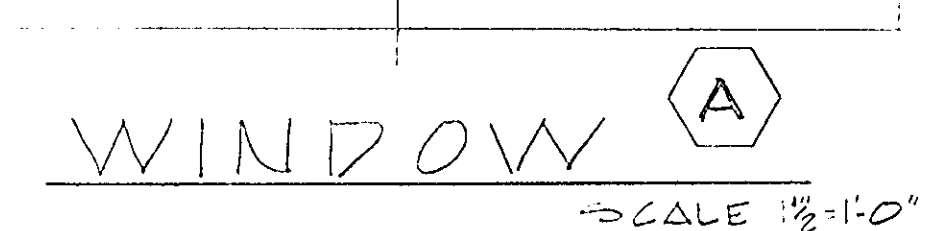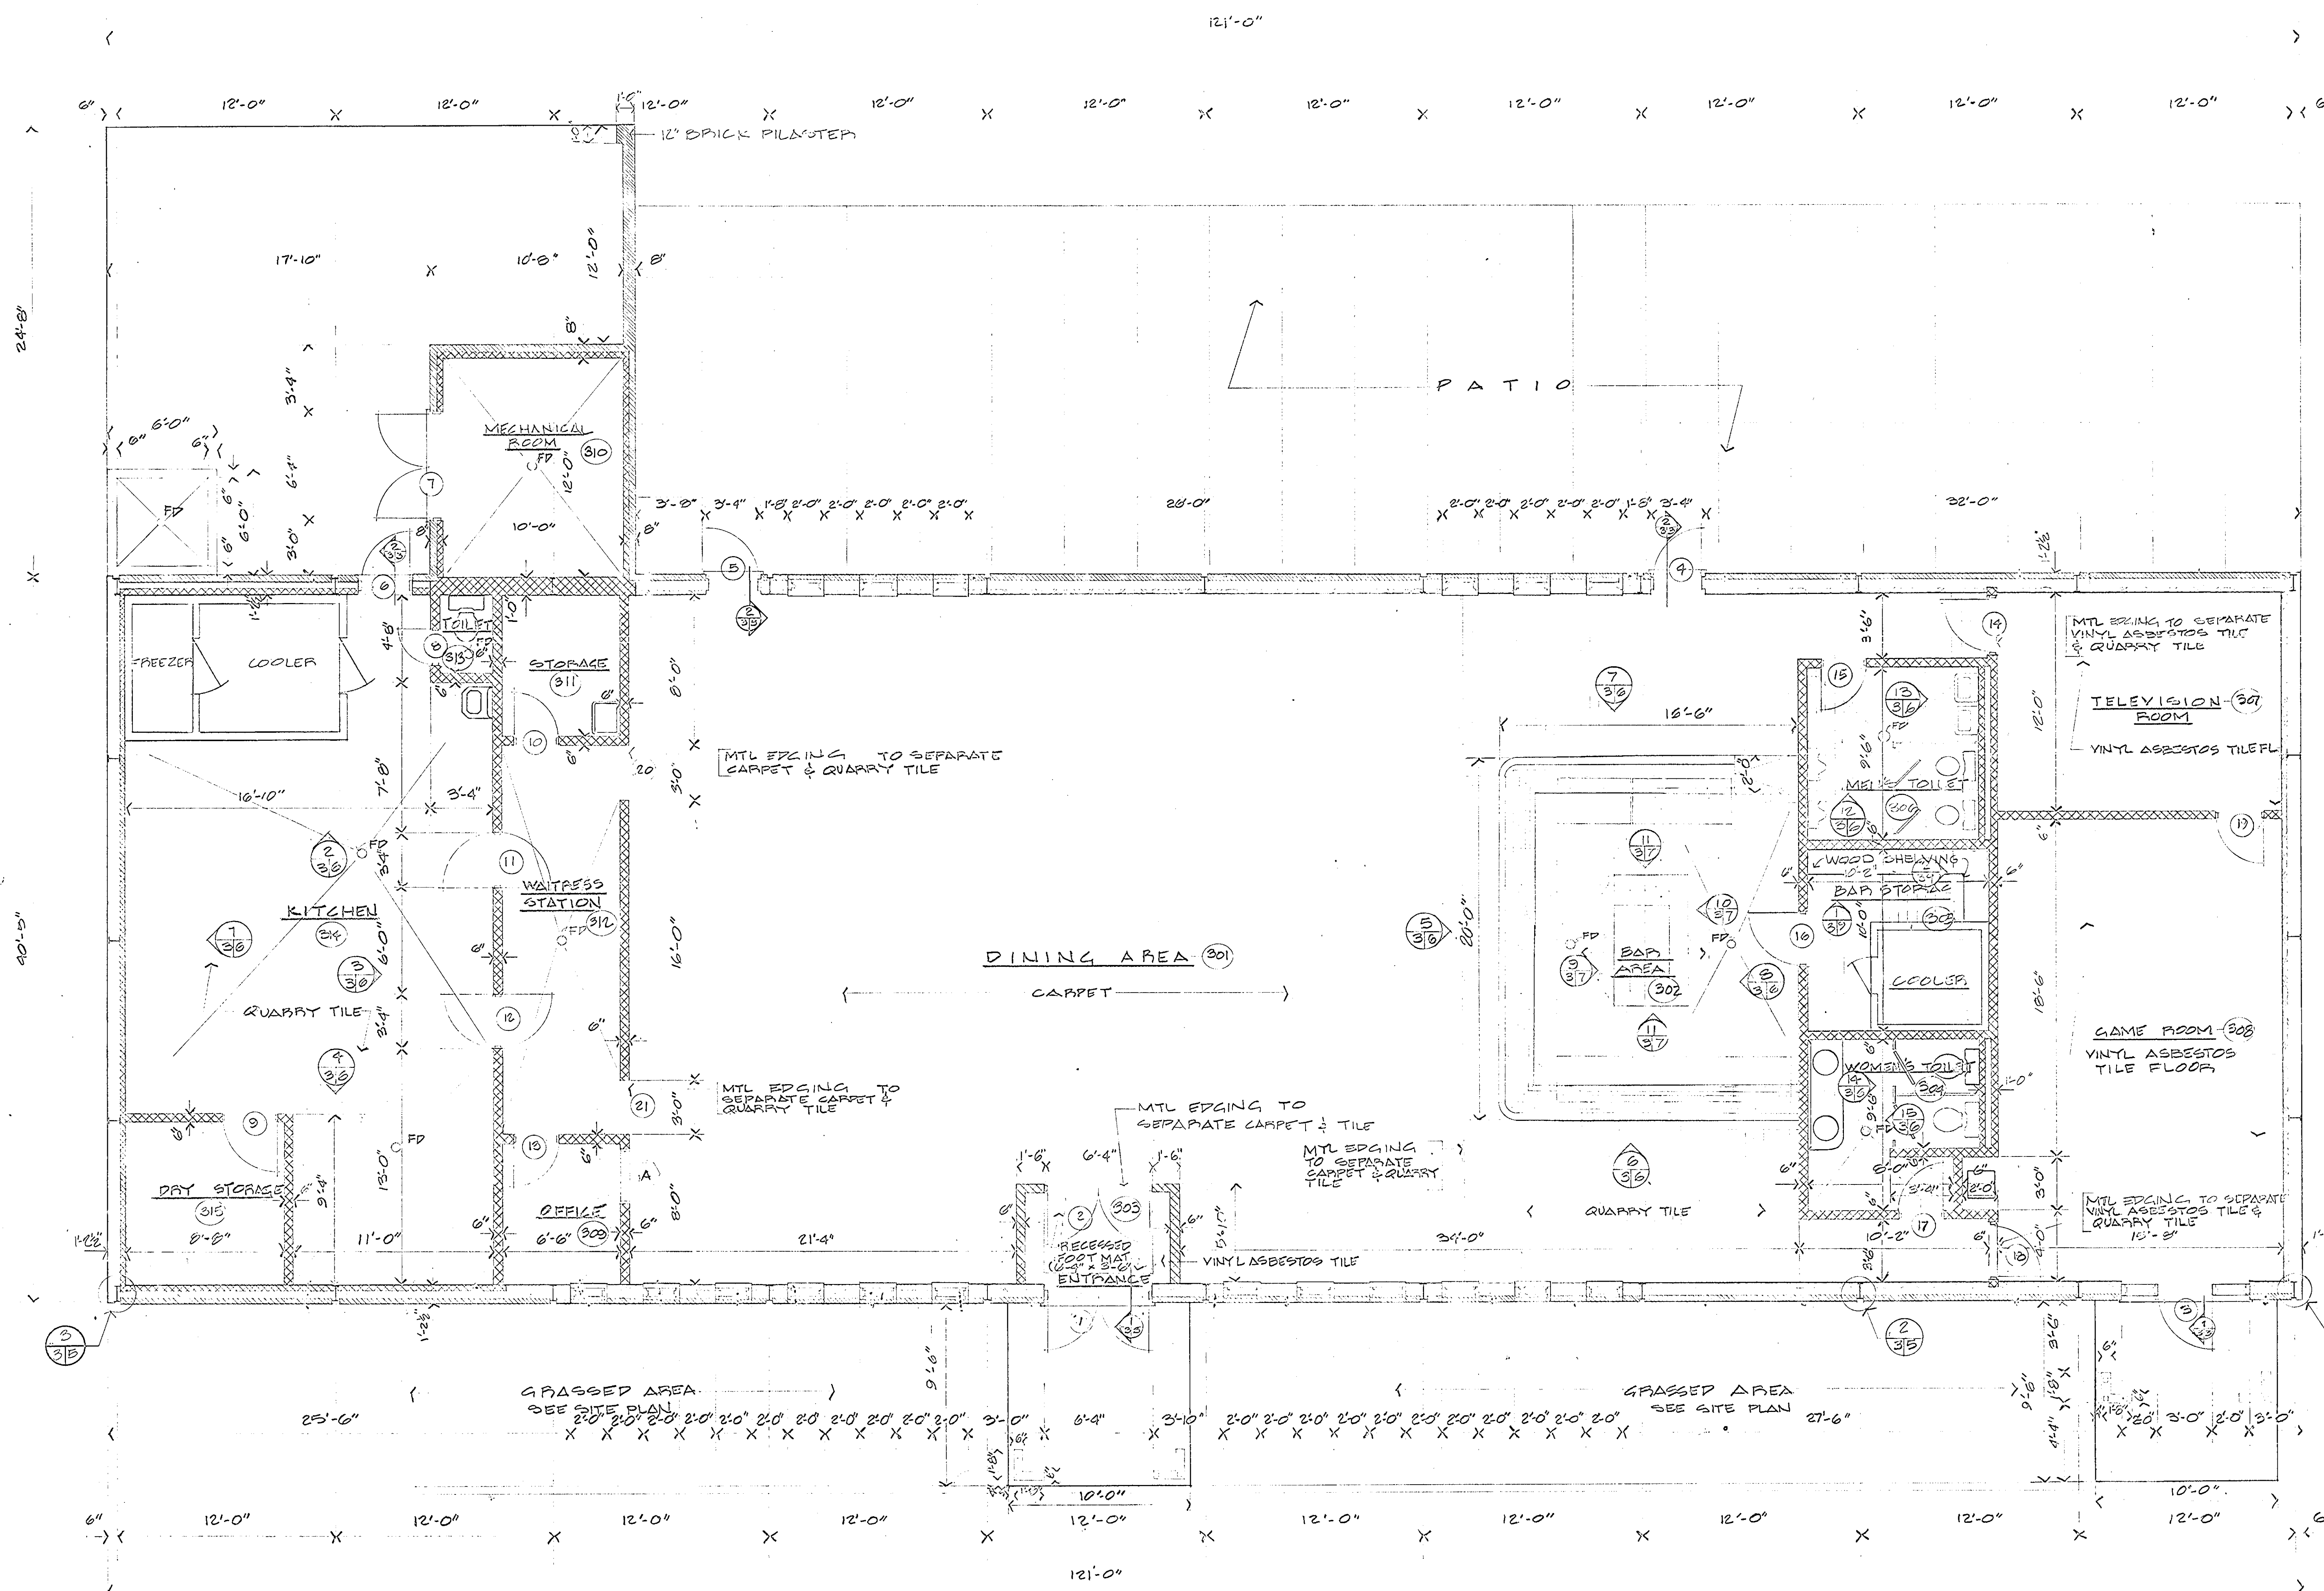


PUBLIC WORKS DEPT. MARINE CORPS BASE CAMP LEJEUNE, N.C.		DEPARTMENT OF THE NAVY NAVAL FACILITIES ENGINEERING COMMAND ATLANTIC DIVISION MARINE CORPS BASE, CAMP LEJEUNE, N.C.	
DESIGNED BY DR. J. H. S. J. H. S.	CHK. BY J. H. S. J. H. S.	NCO CLUB, CAMP GEIGER MARINE CORPS BASE, CAMP LEJEUNE, N.C. FLOOR PLAN & DETAILS	
APPROVED BY J. H. S. J. H. S.	DATE J. H. S. J. H. S.	SIZE F 80091	CODE IDENT NO. 4011886
Satisfactory to J. H. S. J. H. S.		NAVAC DRAWING NO. 4011886	
DATE J. H. S. J. H. S.		CONSTR. CONTR. NO. N62470-75-B-0919	
FOR COMMANDER, NAVAC		SHEET 3 OF 18	

REVISIONS			
SYM	DESCRIPTION	DATE	APPROVED

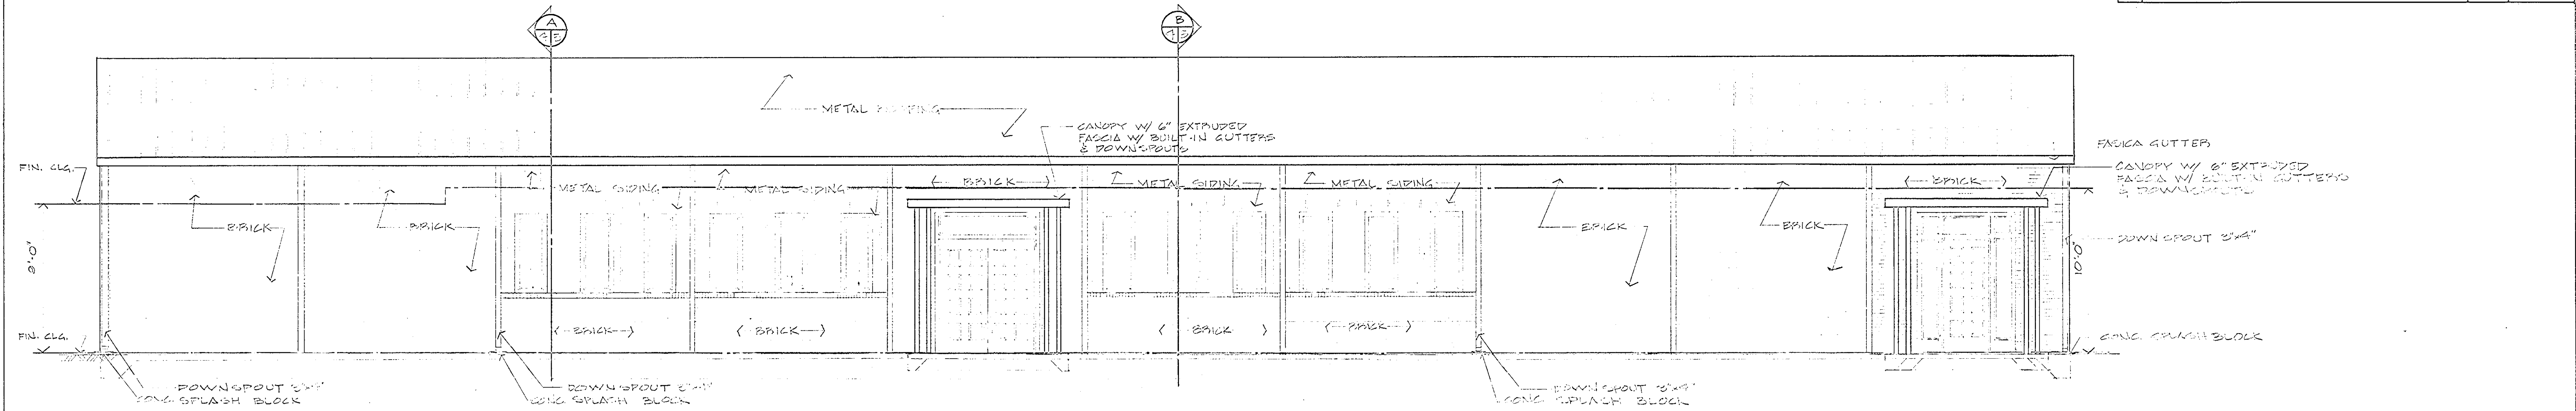


FRONT ELEVATION

SCALE 1/8"=1'-0"

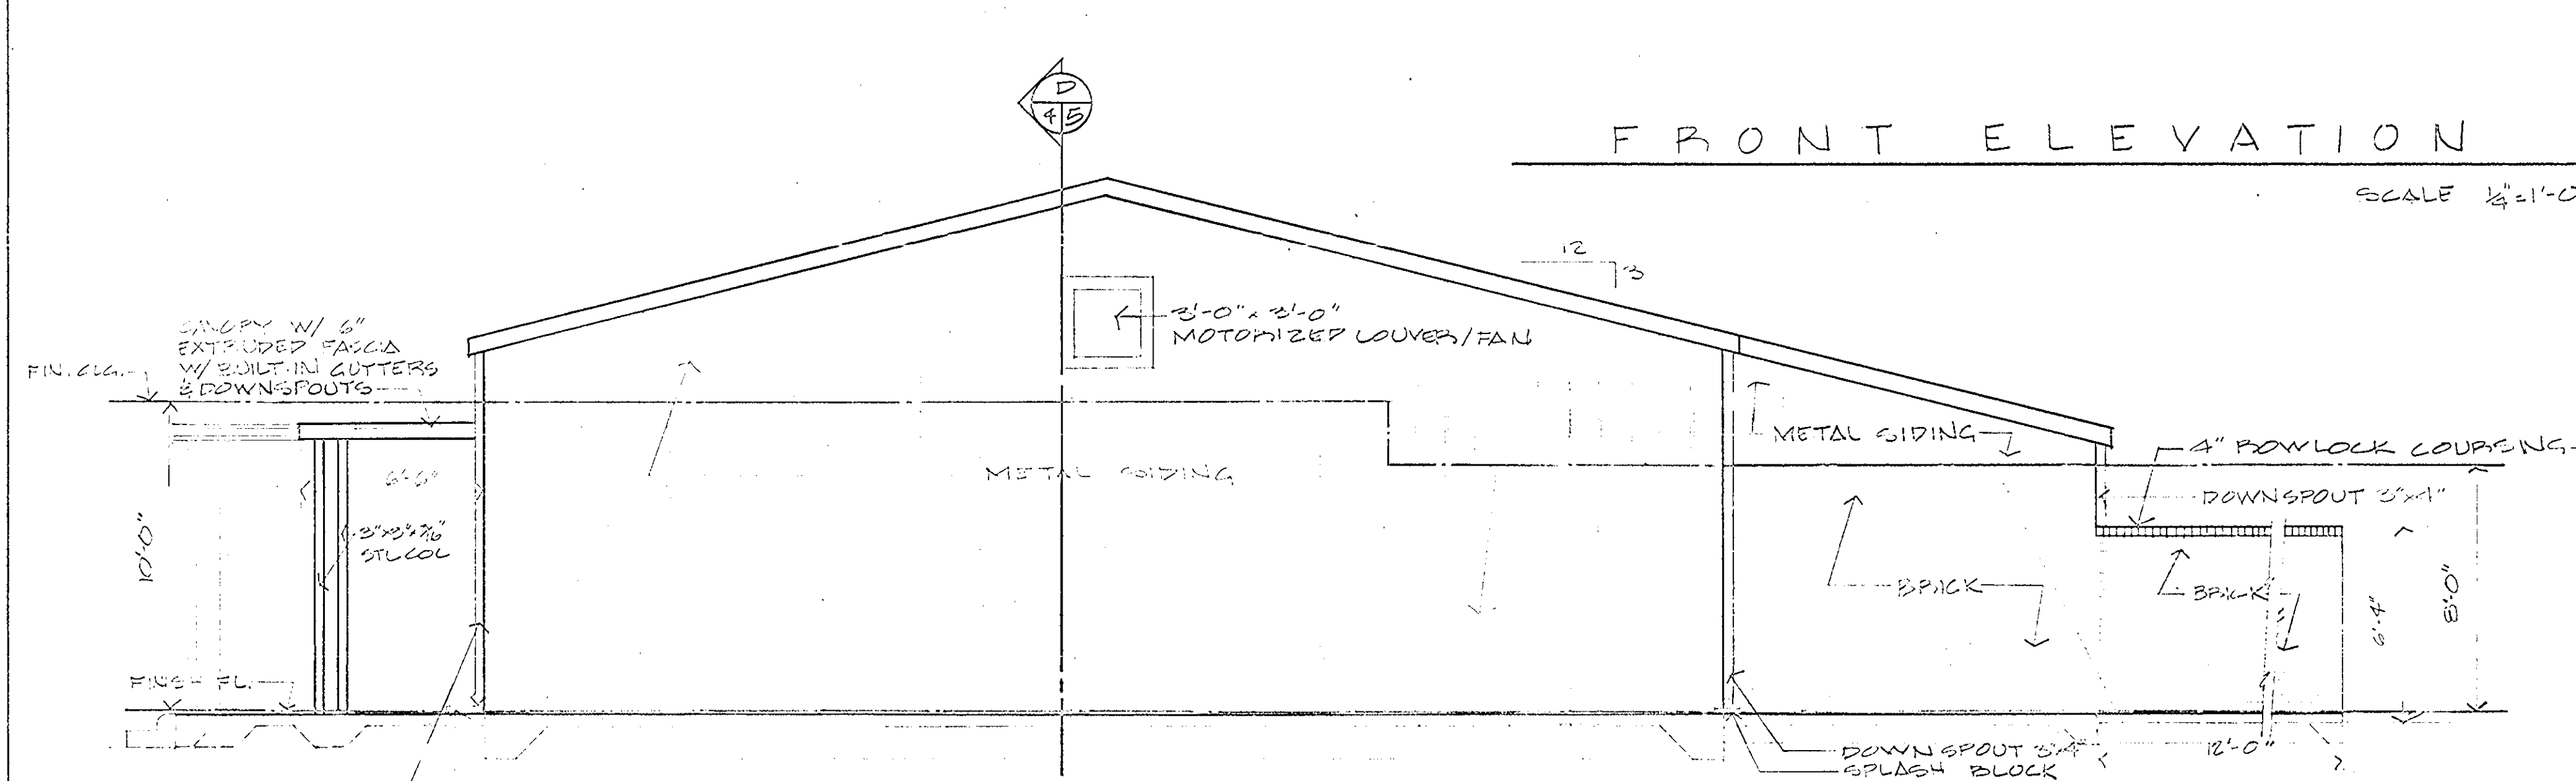


RIGHT SIDE ELEVATION

SCALE 1/8"=1'-0"

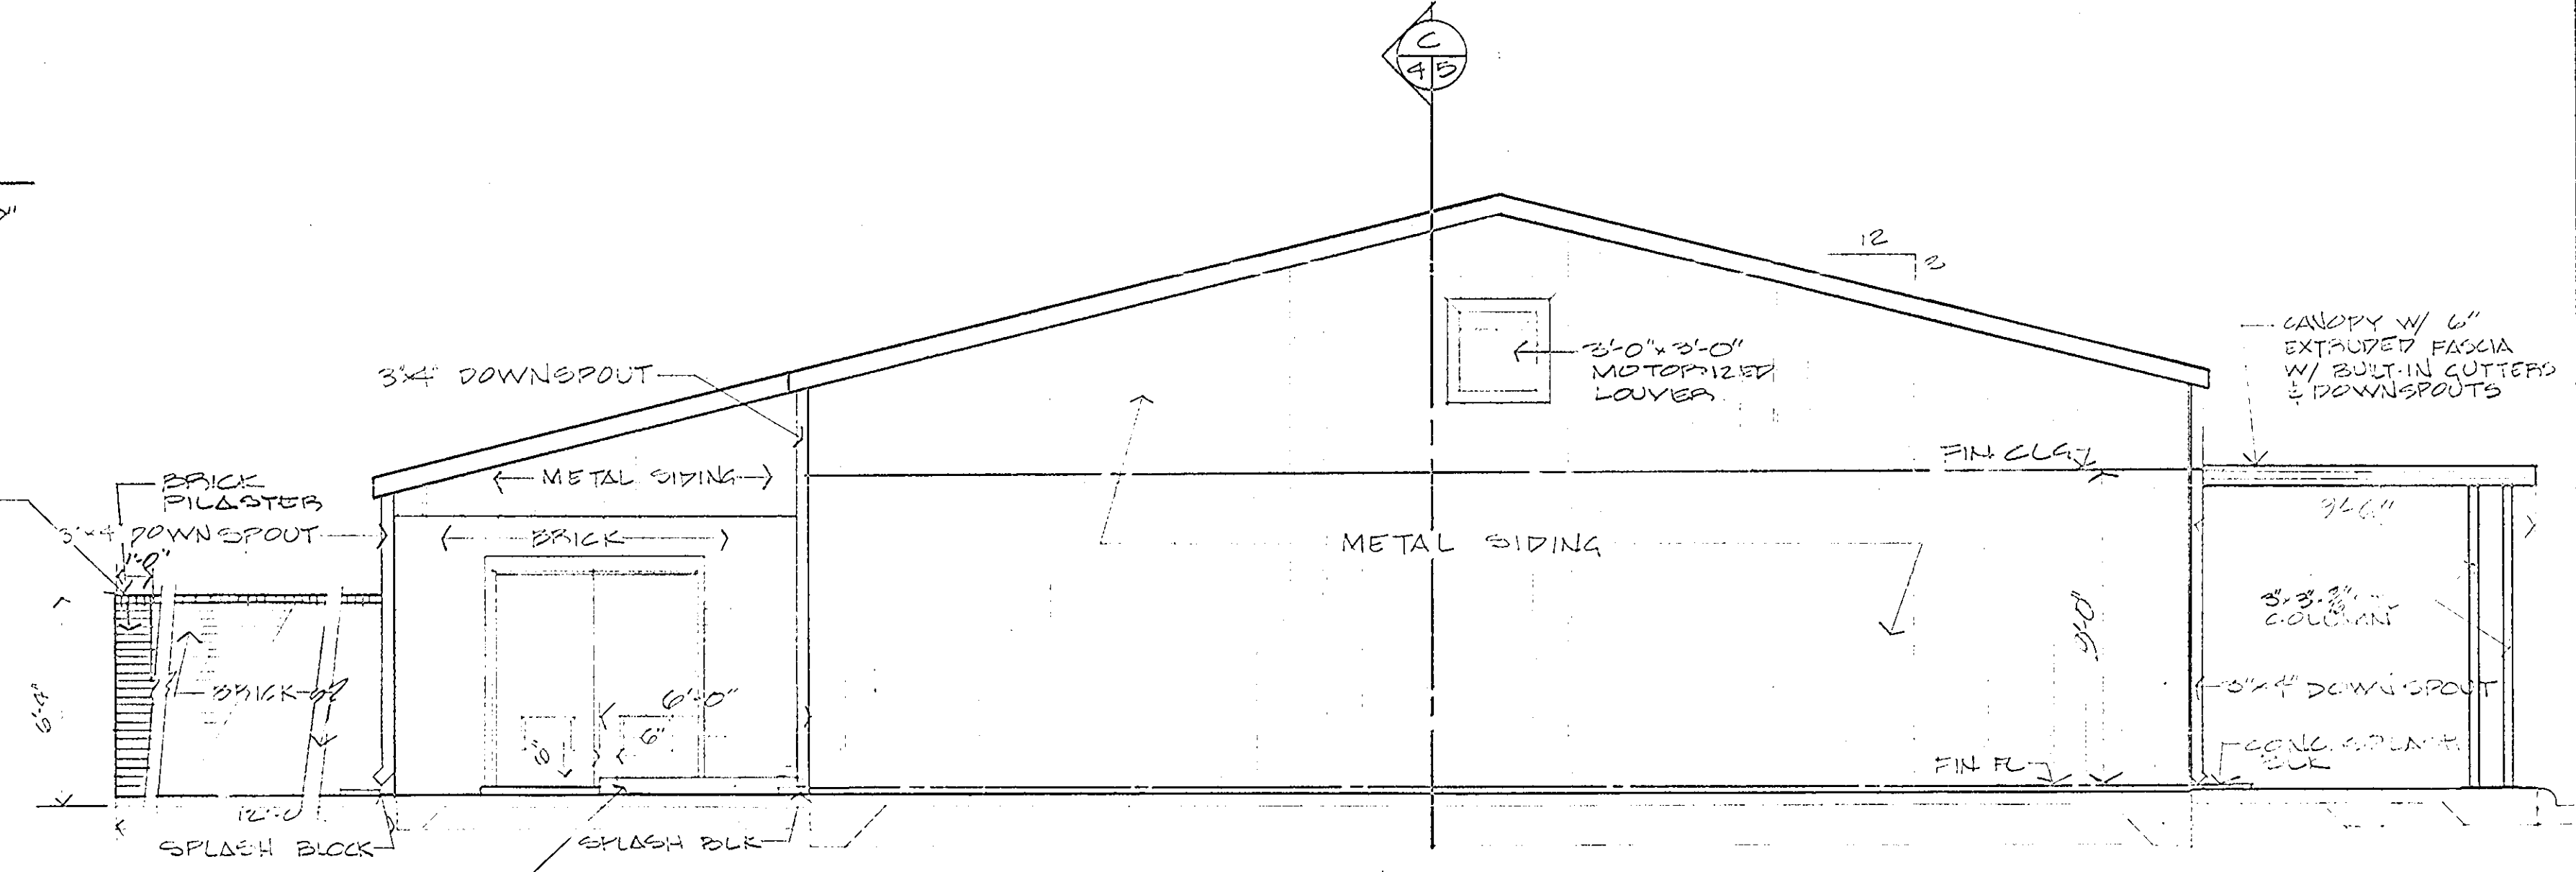


LEFT SIDE ELEVATION

SCALE 1/8"=1'-0"

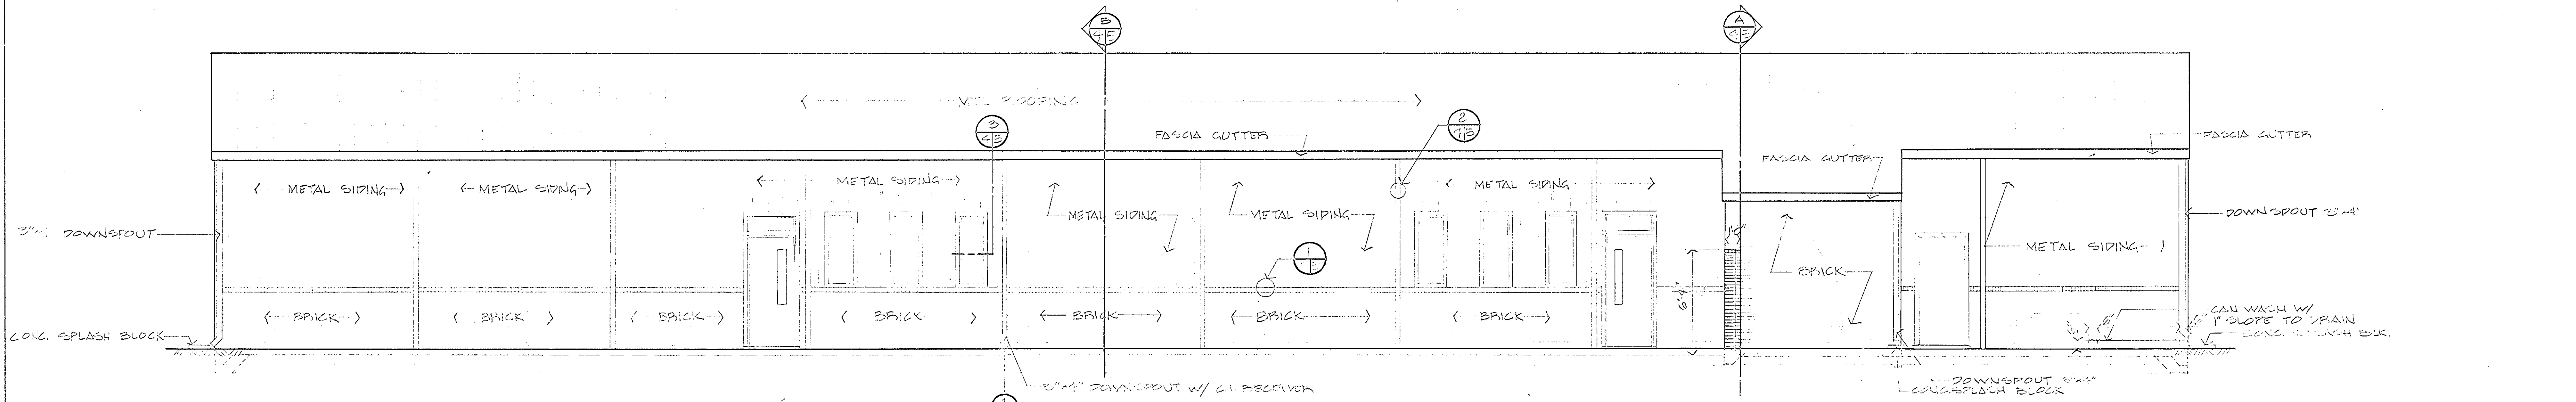

BACK ELEVATION


SCALE 1/8"=1'-0"

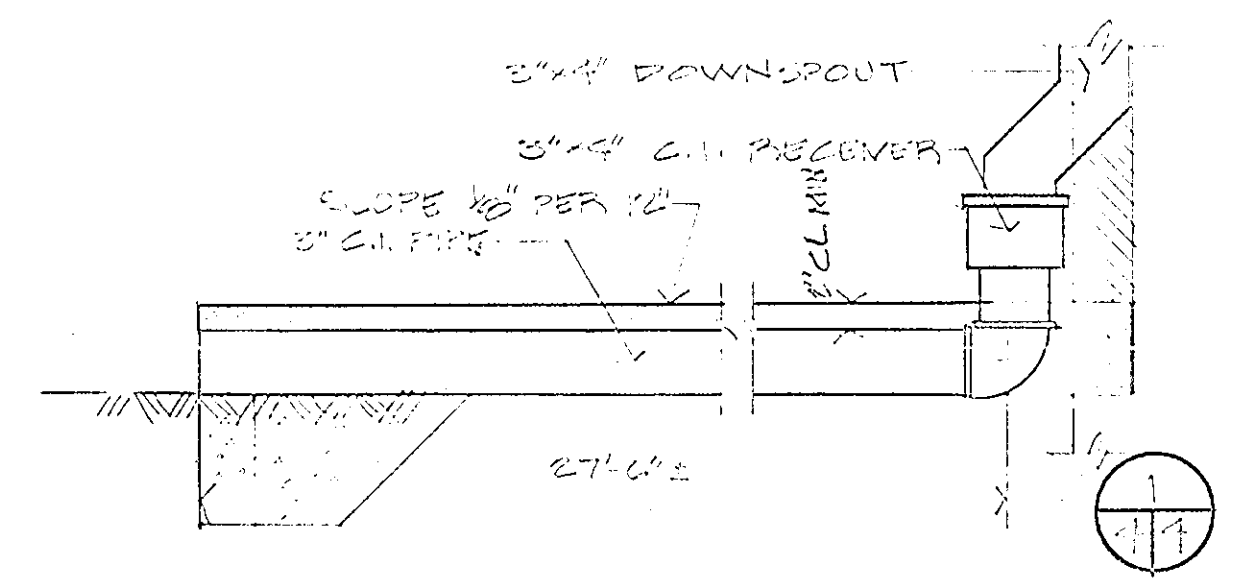

DRAIN DETAIL


SCALE 1/8"=1'-0"

GRAPHIC SCALES

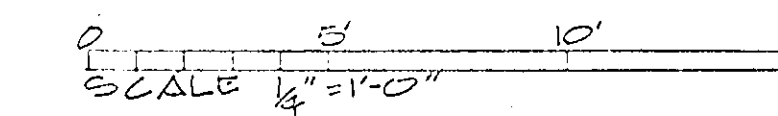

SATISFACTORY TO
[Signature]
DATE 26 April 76





PUBLIC WORKS DEPT. MARINE CORPS BASE CAMP LEJEUNE, N.C.		DEPARTMENT OF THE NAVY NAVAL FACILITIES ENGINEERING COMMAND ATLANTIC DIVISION MARINE CORPS BASE, CAMP LEJEUNE, N.C.	
DES/76	DR/76	CHK/76	DATE/76
APPROVED <i>[Signature]</i>		DATE/76	
PUBLIC WORKS OFFICER		SATISFACTORY TO	
COMMANDING GENERAL		DATE	
EFD		RVD	
NO		DIR	
APPROVED <i>[Signature]</i>		DATE/76	
FOR COMMANDER, NAVFAC		SCALE GRAPHIC SPEC 05-75-0919	
SIZE CODE IDENT NO F 80091		NAVFAC DRAWING NO 4011887	
CONSTR CONTR NO N62470-75-B-0919		SHEET 4 OF 18	
LANTDIV DWG NO			

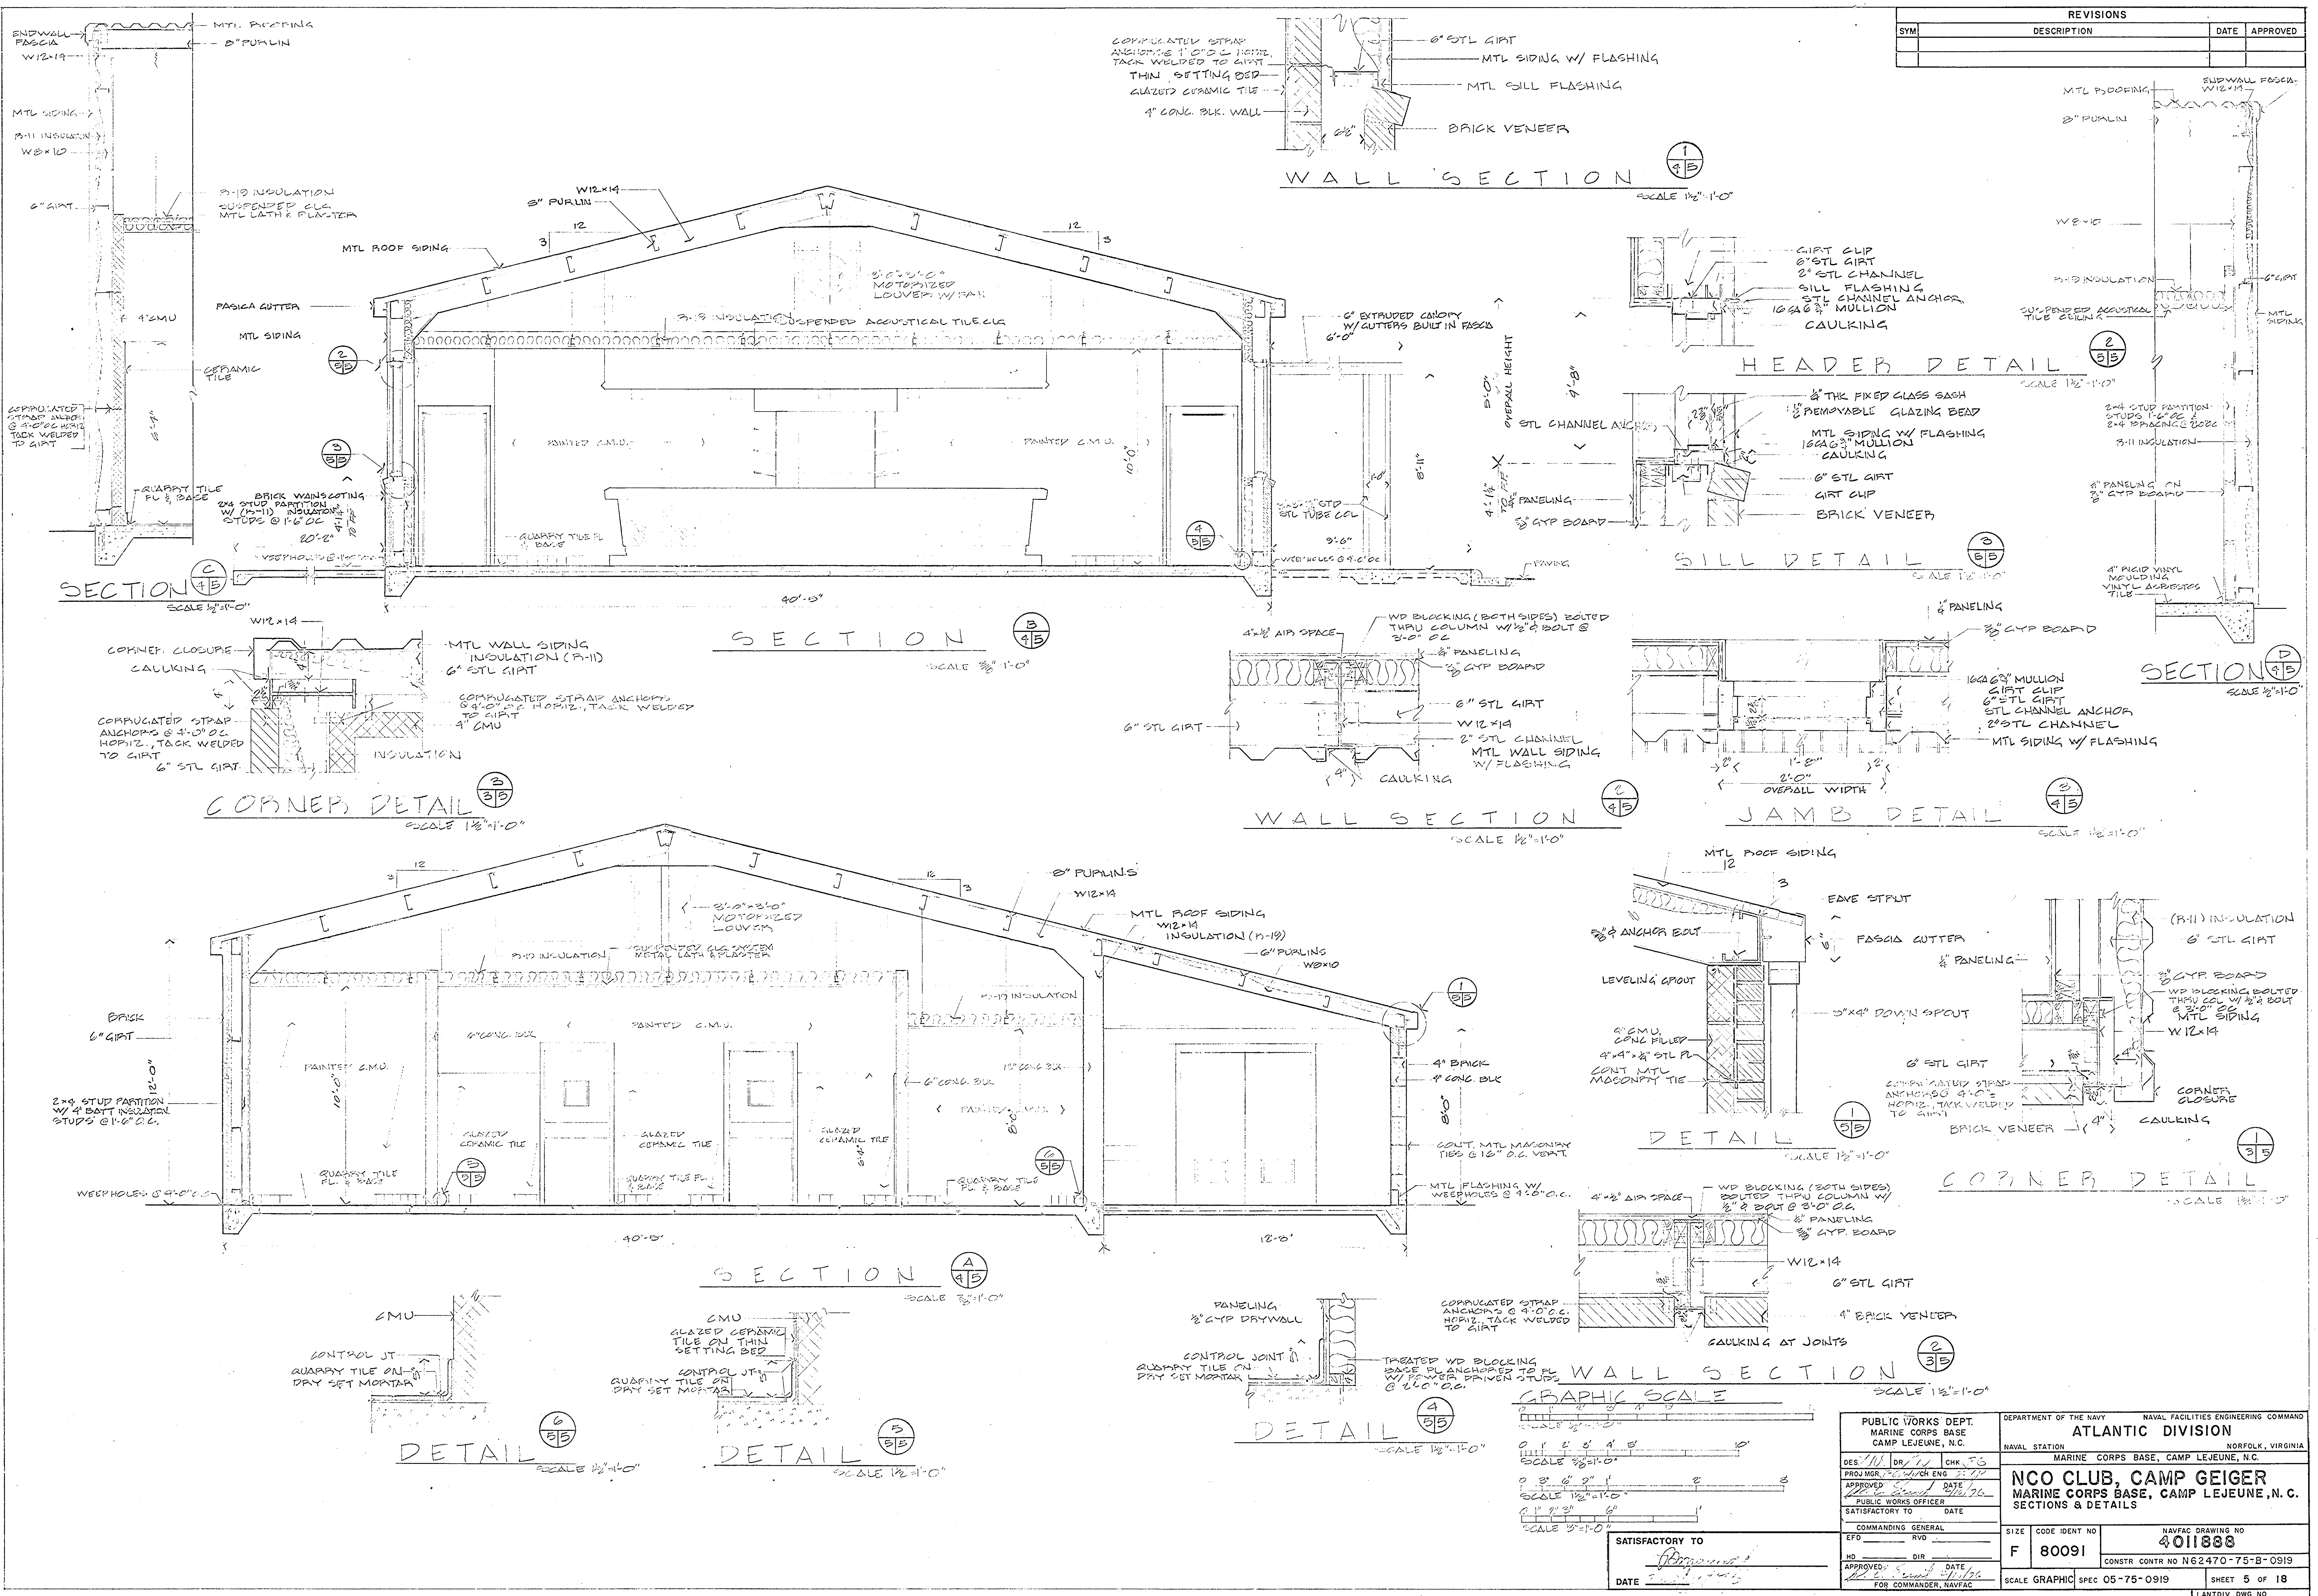

REVISIONS			
SYM.	DESCRIPTION	DATE	APPROVED














PUBLIC WORKS DEPT. MARINE CORPS BASE CAMP LEJEUNE, N.C.		DEPARTMENT OF THE NAVY NAVAL FACILITIES ENGINEERING COMMAND ATLANTIC DIVISION	
DESIGNED BY: [Signature] CHECKED BY: [Signature] APPROVED BY: [Signature] DATE: 11/1/70		MARINE CORPS BASE, CAMP LEJEUNE, N.C. NCO CLUB, CAMP GEIGER MARINE CORPS BASE, CAMP LEJEUNE, N.C. SECTIONS & DETAILS	
Satisfactory to: [Signature] DATE: 11/1/70		SIZE: 80091 CODE IDENT NO: 4011888 CONSTR CONTR NO: N62470-75-B-0919	
COMMANDING GENERAL RVD NO. 1 APPROVED BY: [Signature] DATE: 11/1/70 FOR COMMANDER, NAVFAC		SCALE GRAPHIC SPEC 05-75-0919 SHEET 5 OF 18 LAND DIV DWG NO.	

REVISIONS			
SYM	DESCRIPTION	DATE	APPROVED

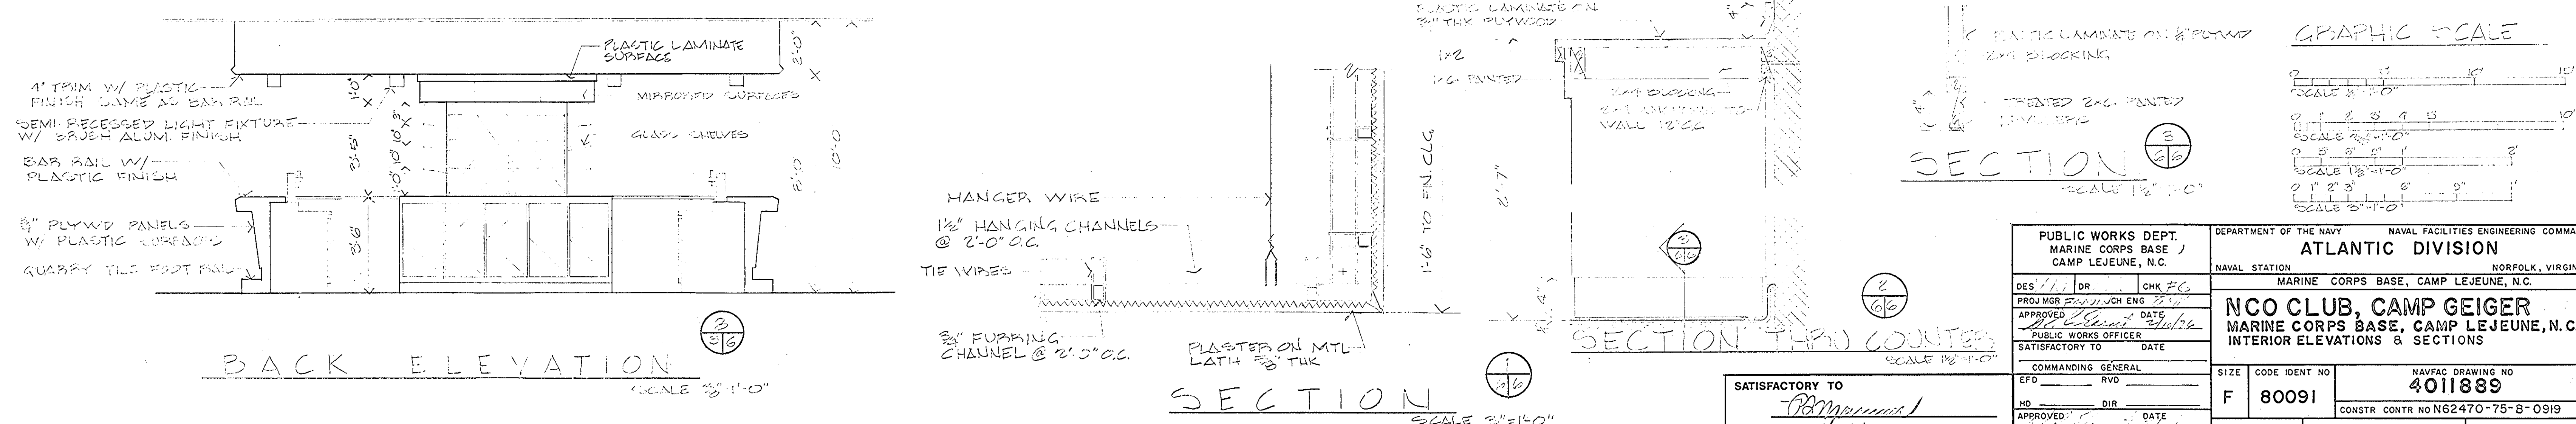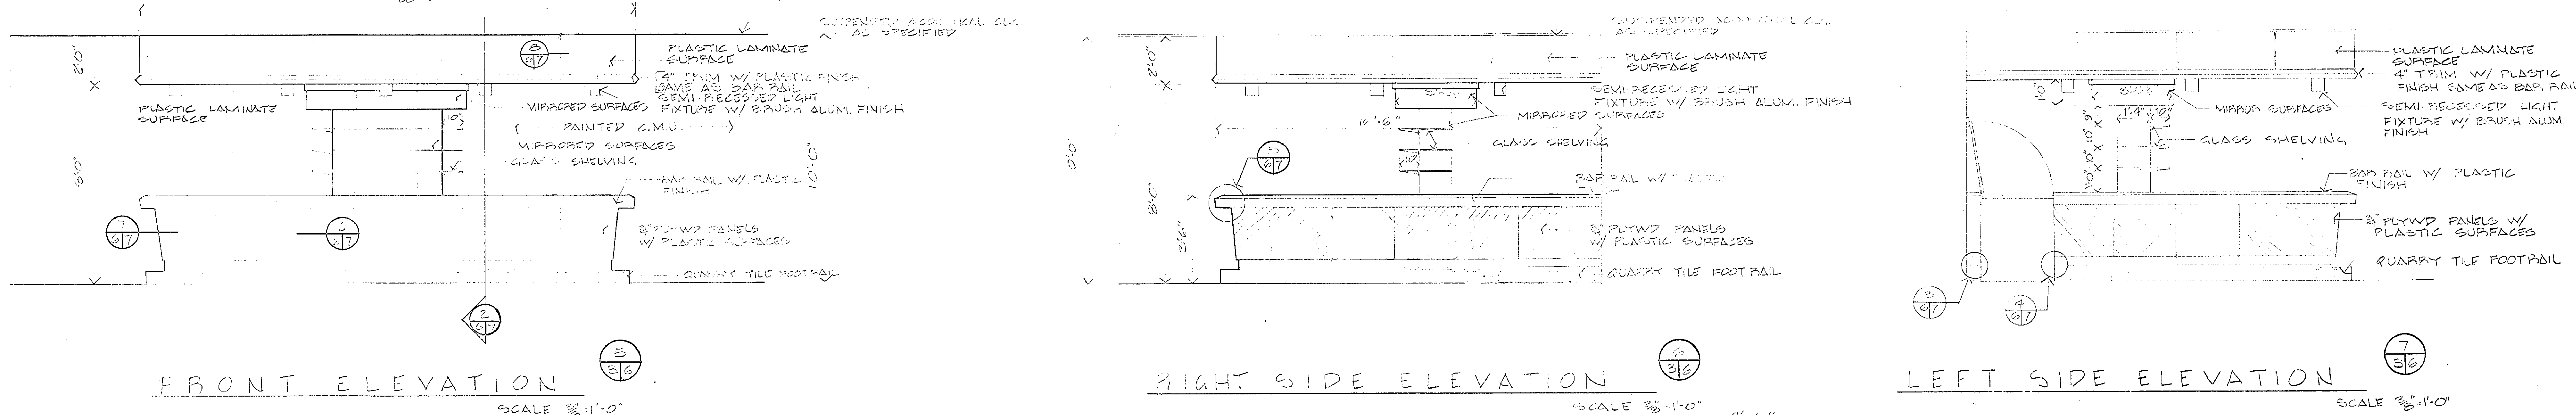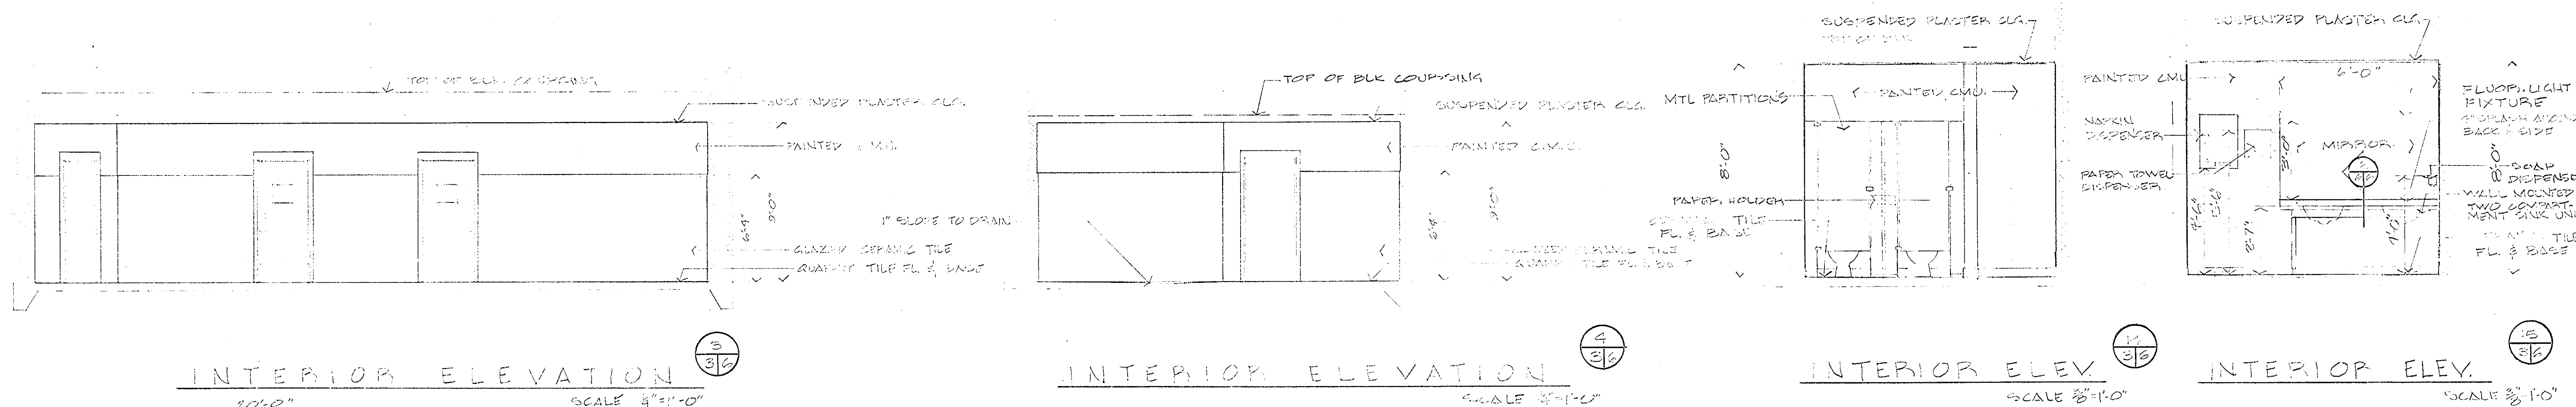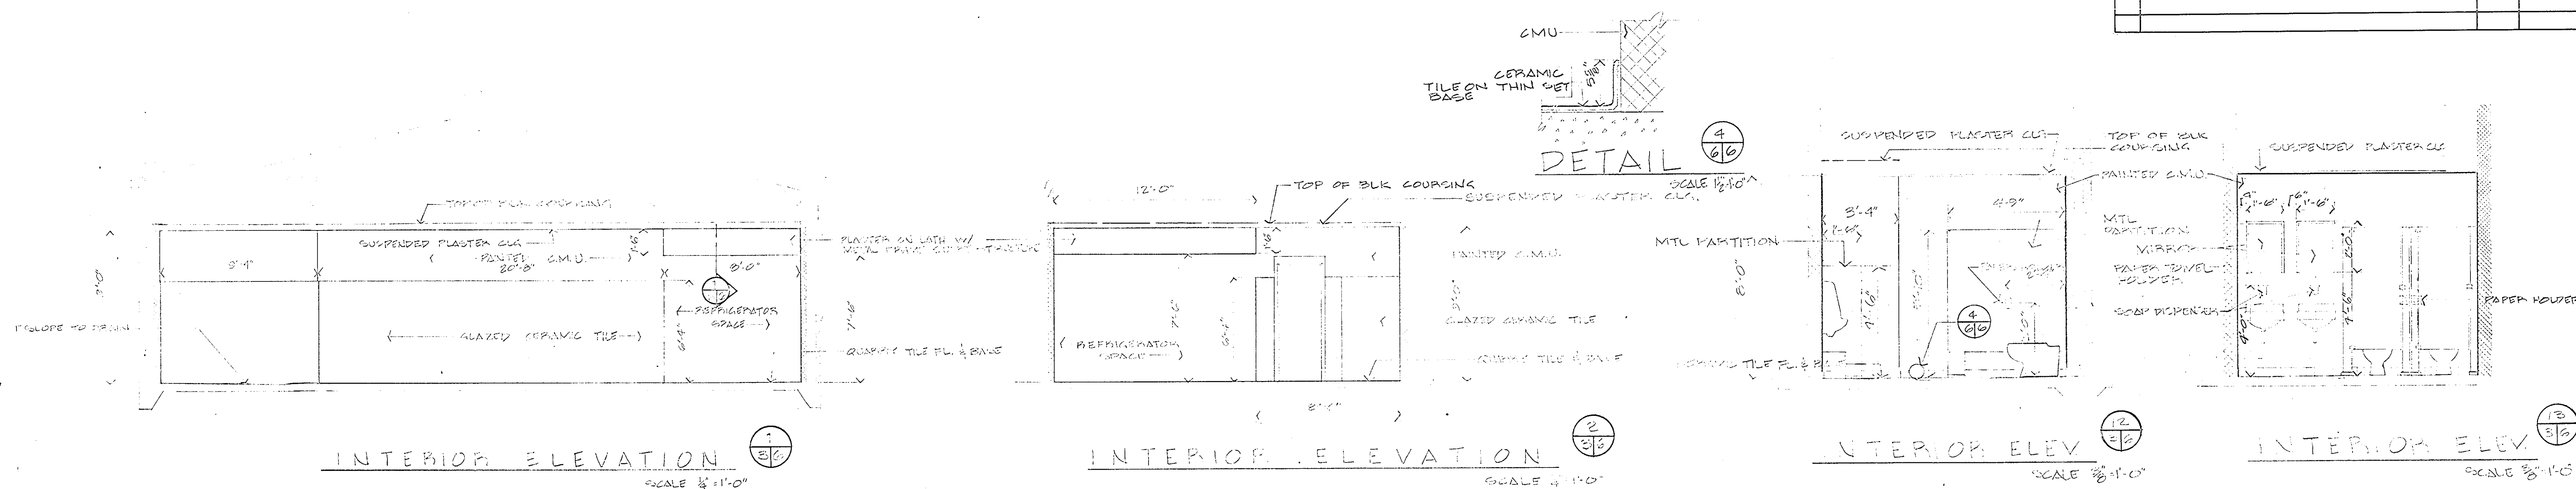

PUBLIC WORKS DEPT. MARINE CORPS BASE CAMP LEJEUNE, N.C.			DEPARTMENT OF THE NAVY			NAVAL FACILITIES ENGINEERING COMMAND		
						ATLANTIC DIVISION		
NAVAL STATION						NORFOLK, VIRGINIA		
MARINE CORPS BASE, CAMP LEJEUNE, N.C.								
DES <u>FCG</u>	DR	CHK <u>FCG</u>	NCO CLUB, CAMP GEIGER MARINE CORPS BASE, CAMP LEJEUNE, N.C. INTERIOR ELEVATIONS & SECTIONS					
PROJECT PROGRAM <u>ARCH ENG</u>								
APPROVED _____ DATE _____								
BY <u>PUBLIC WORKS OFFICER</u>								
SATISFACTORY TO _____ DATE _____								
COMMANDING GENERAL			SIZE			NAVAF DRAWING NO		
EFD _____ RVD _____			F			401889		
MD _____ DIR _____			8009I			CONSTR CONTR NO N62470-75-B-0919		
APPROVED _____ DATE _____			SCALE GRAPHIC			SPEC 05-75-0919		
FOR COMMANDER, NAVAF						SHEET 6 OF 18		


REVISIONS			
SYM	DESCRIPTION	DATE	APPROVED

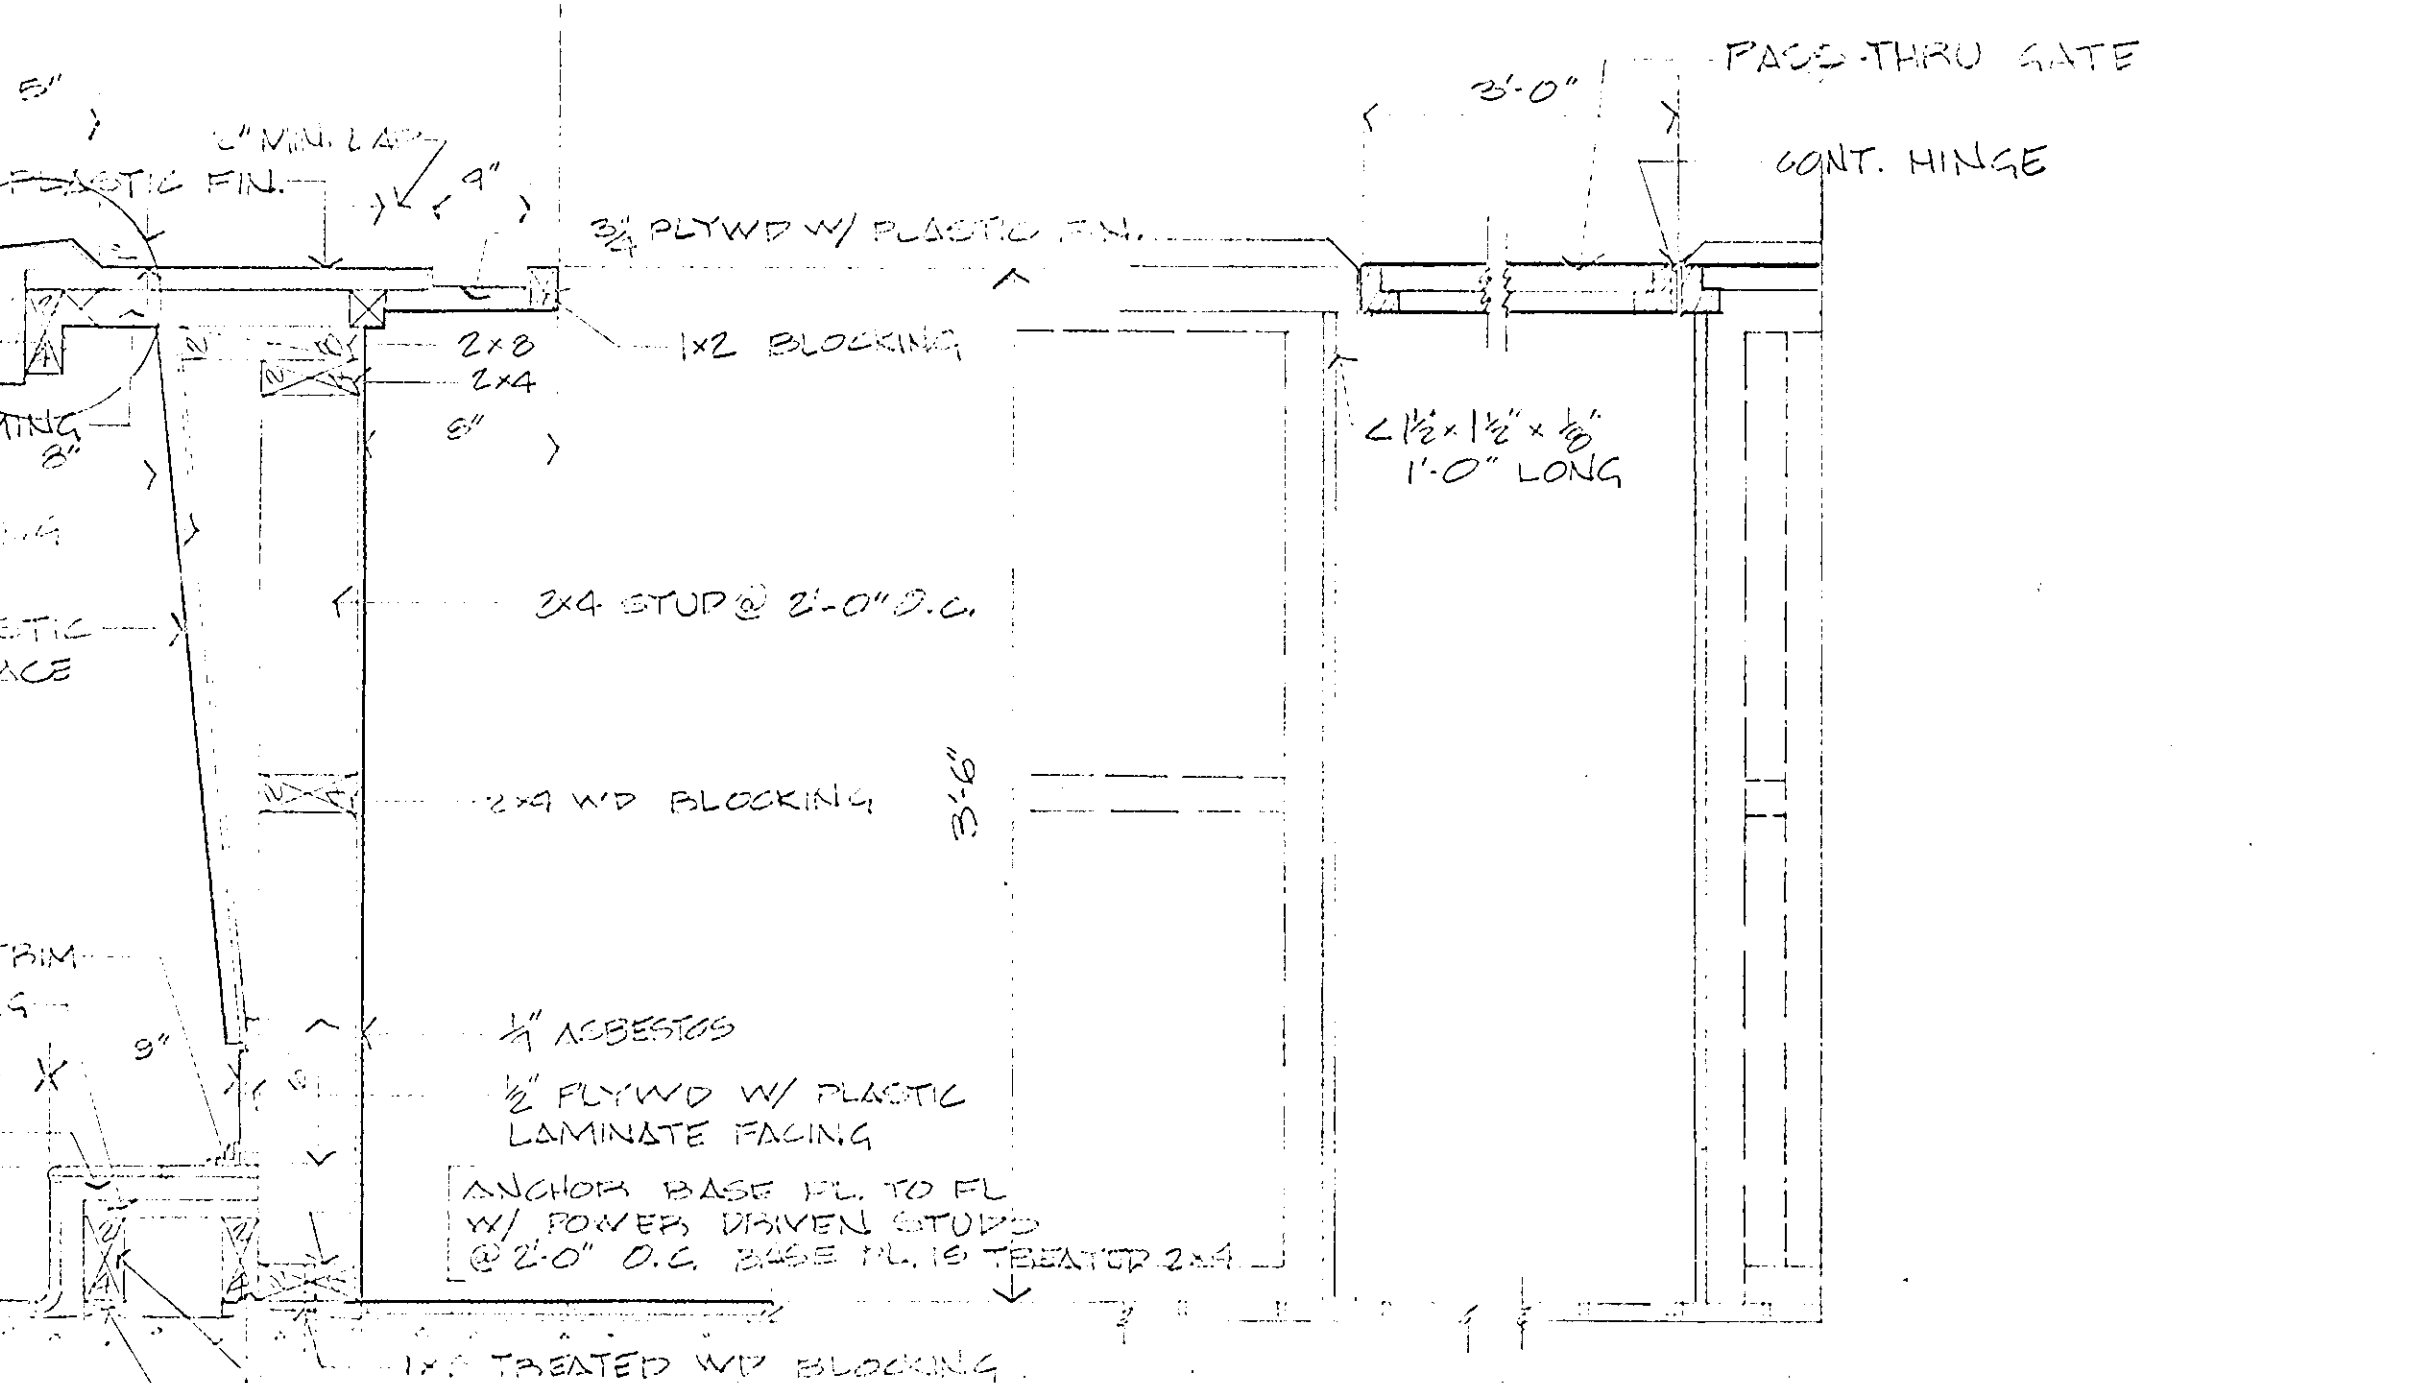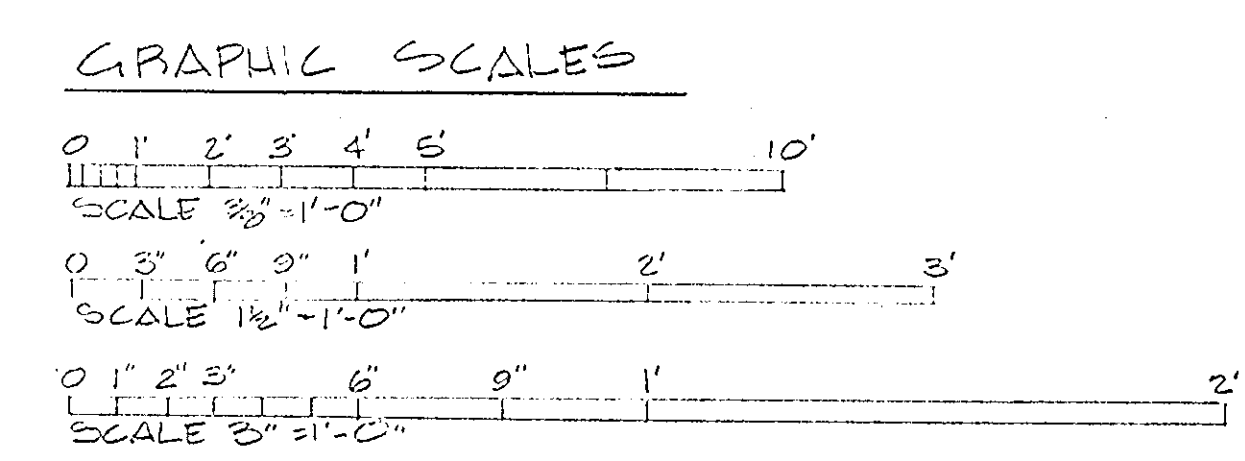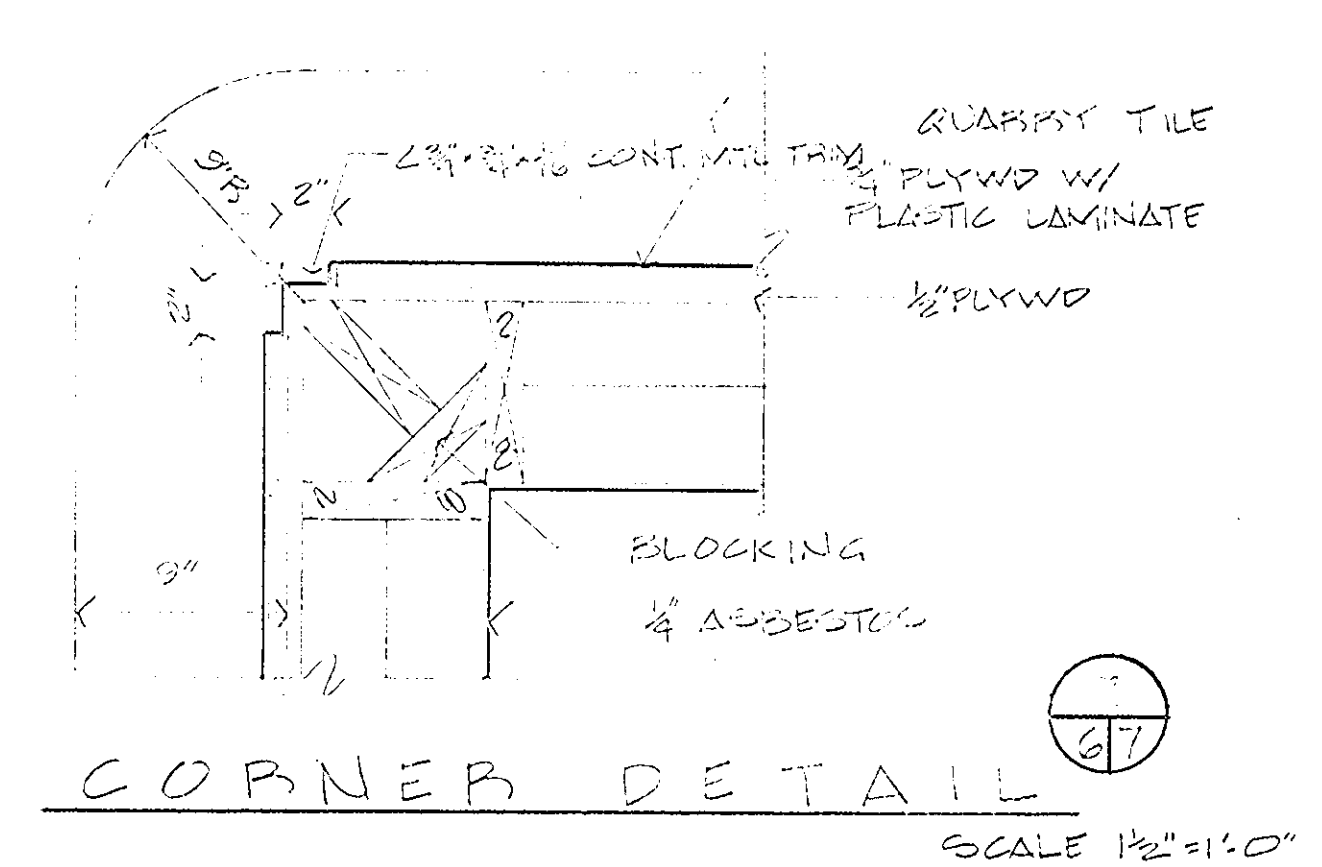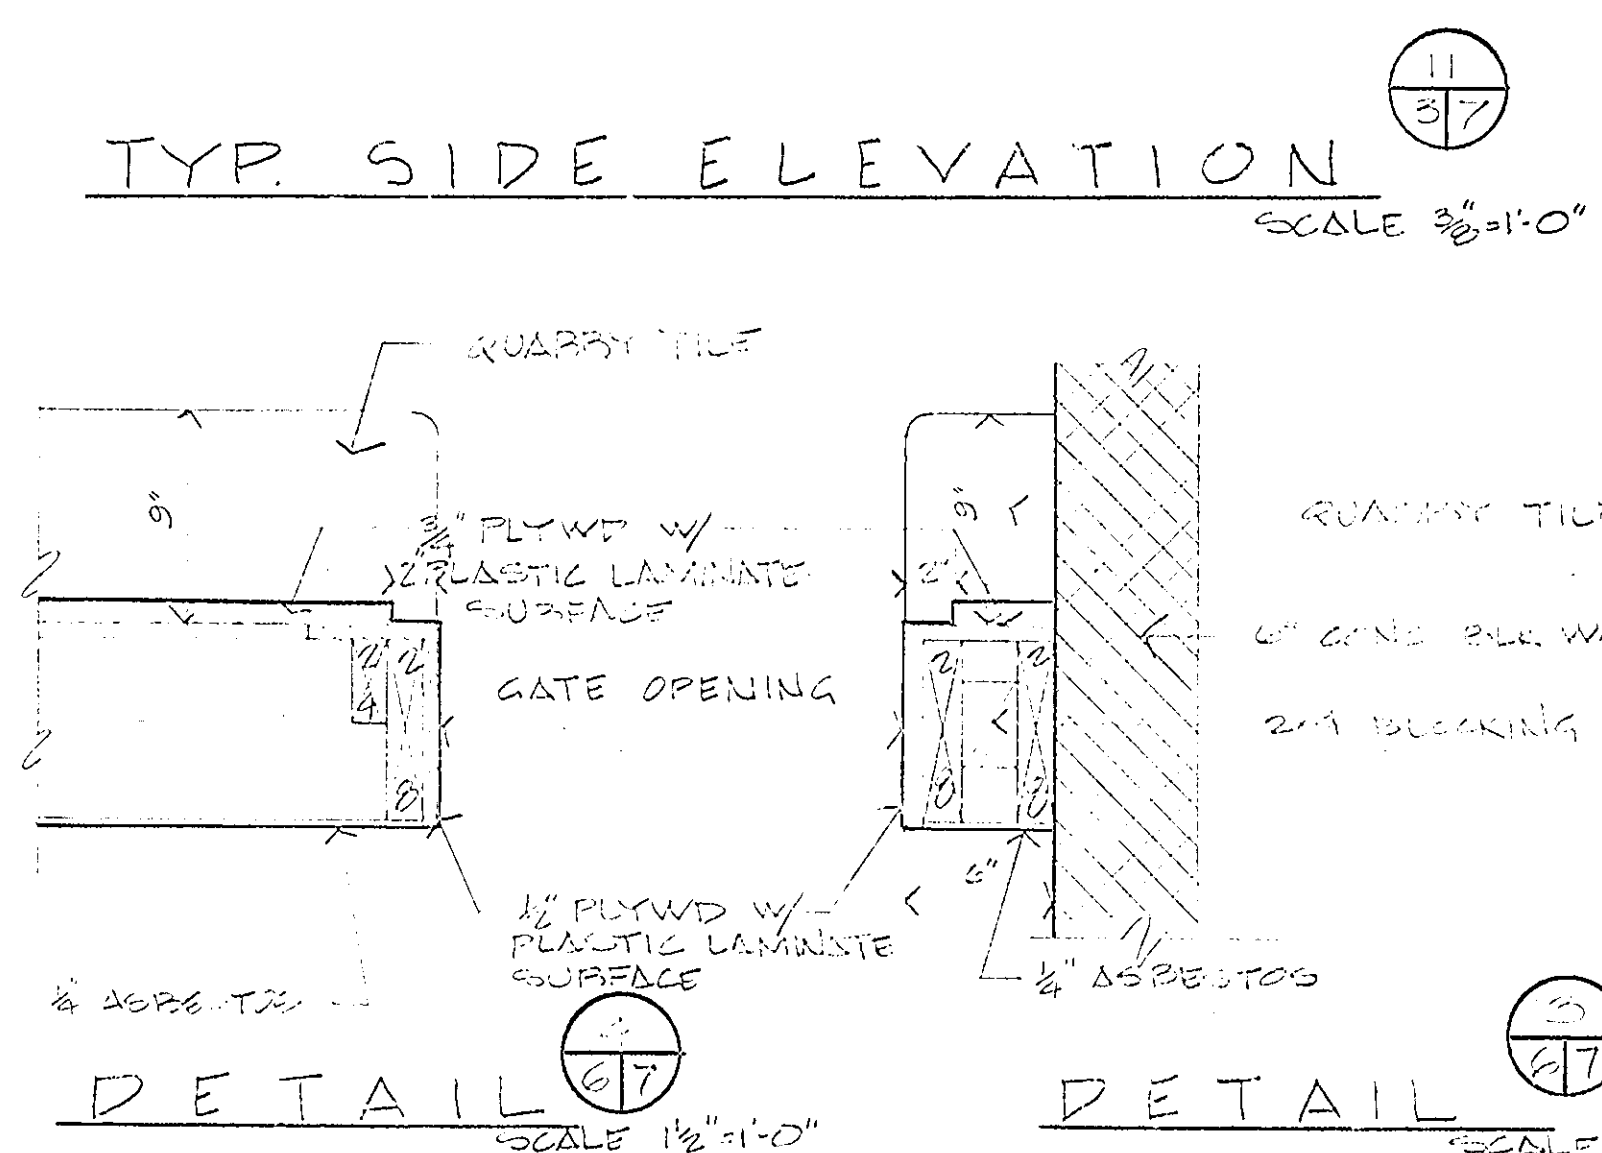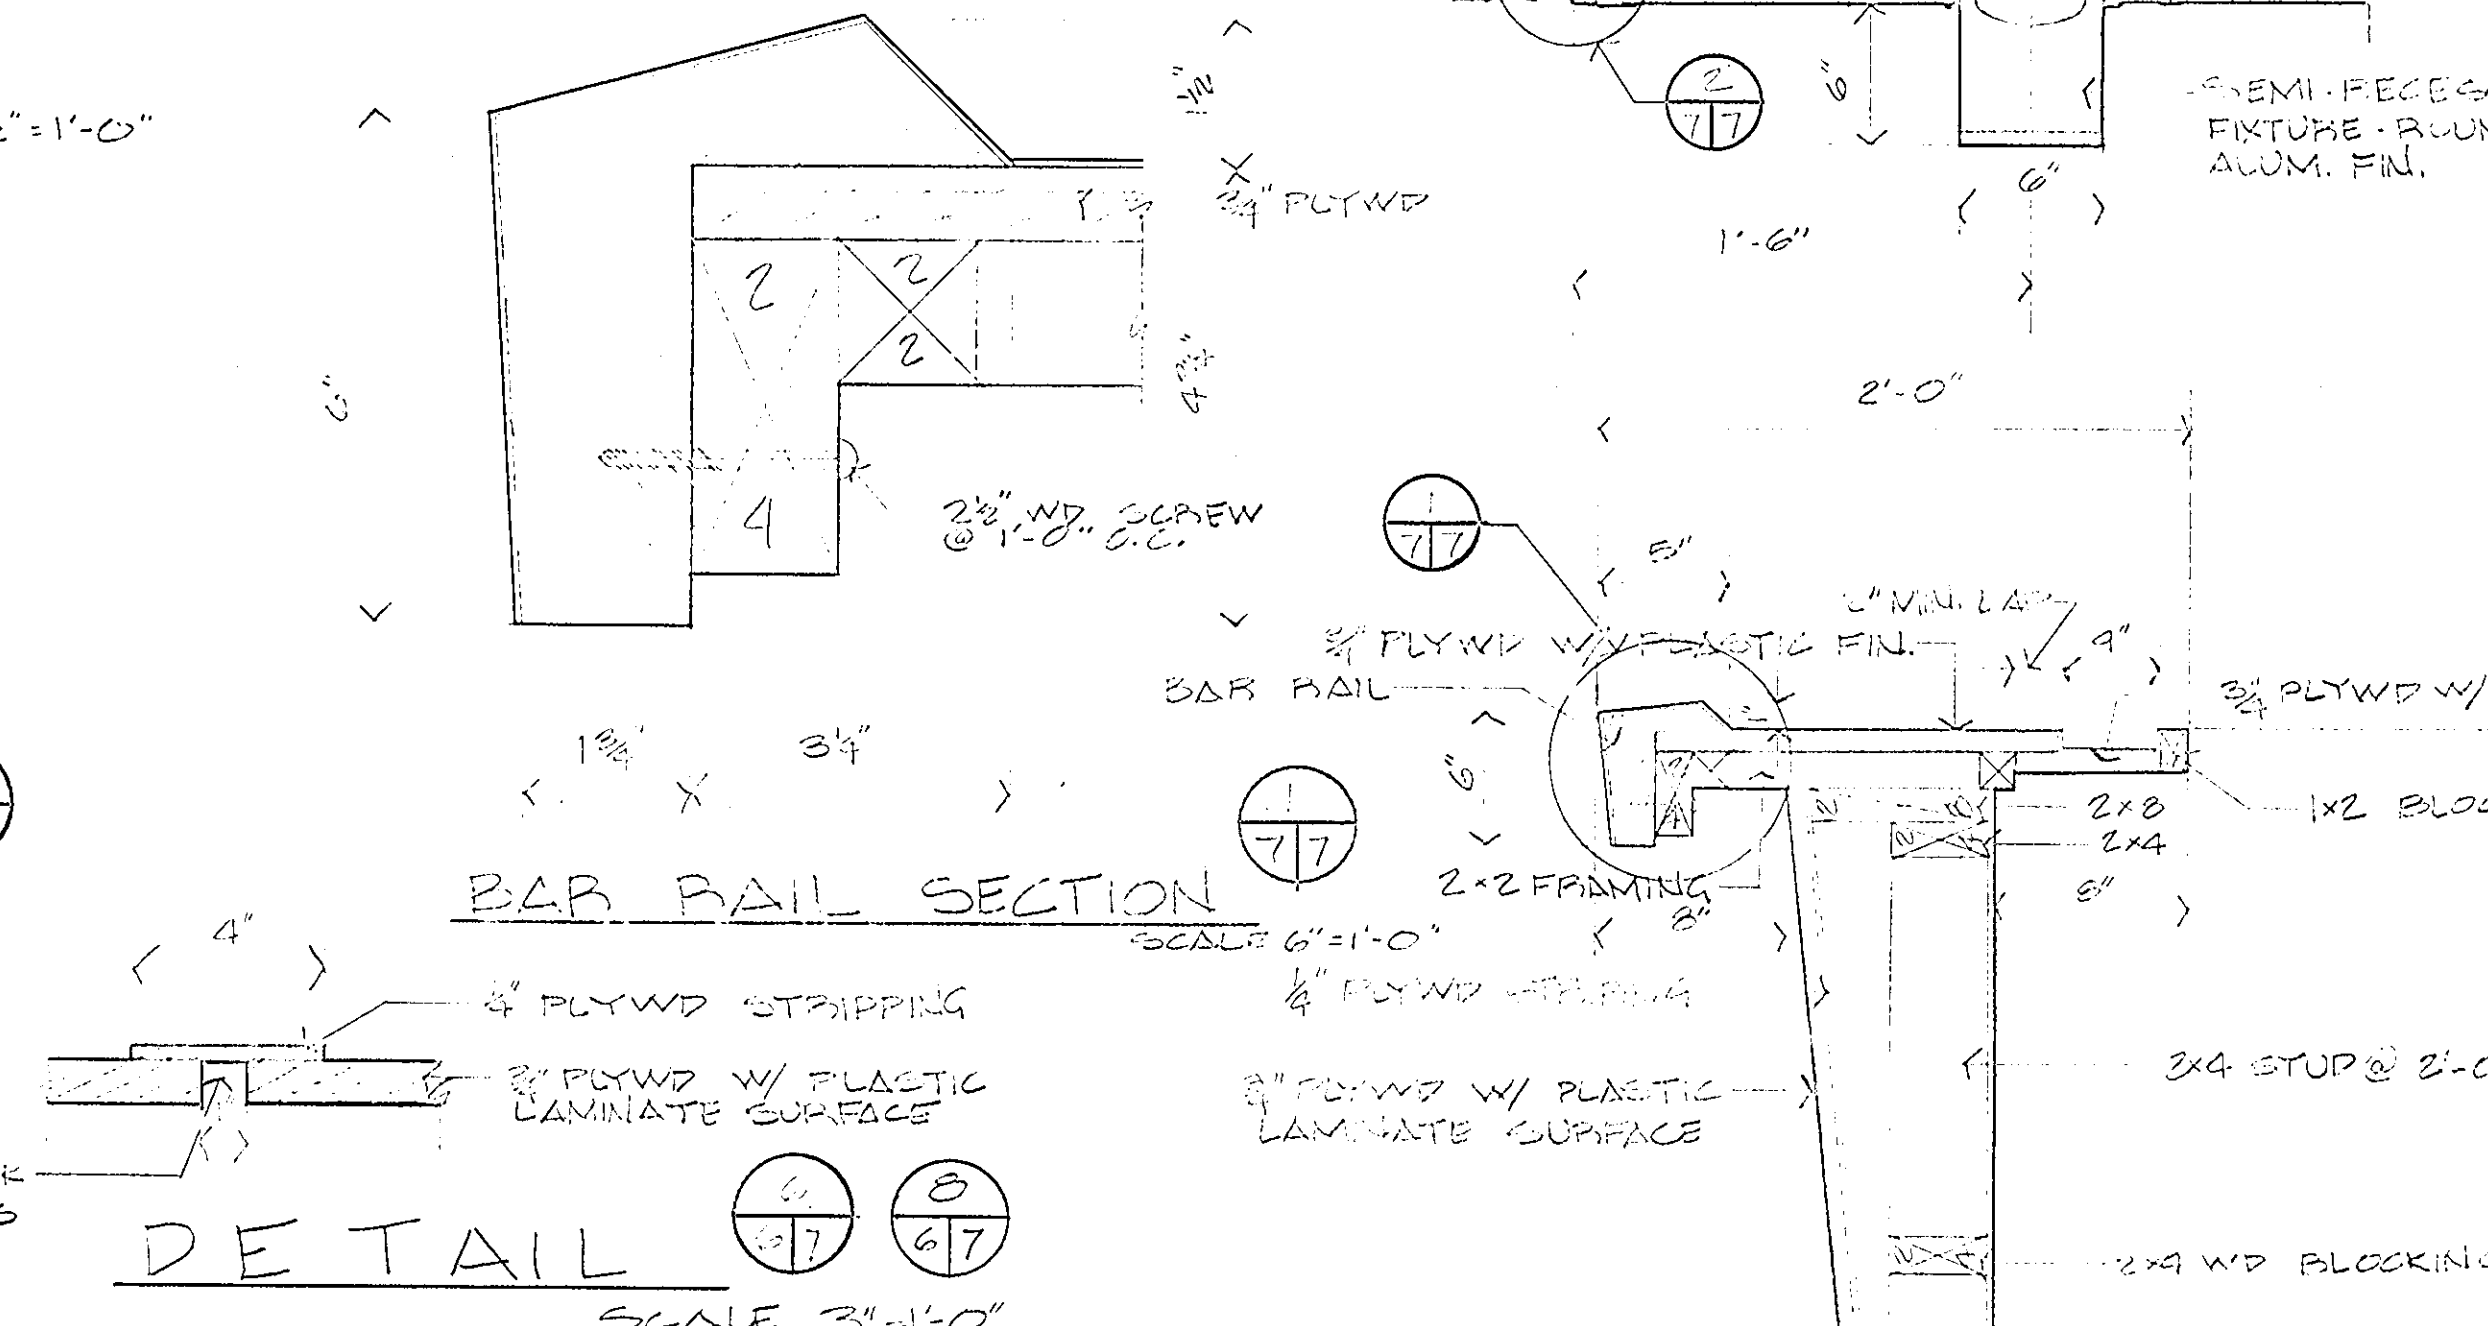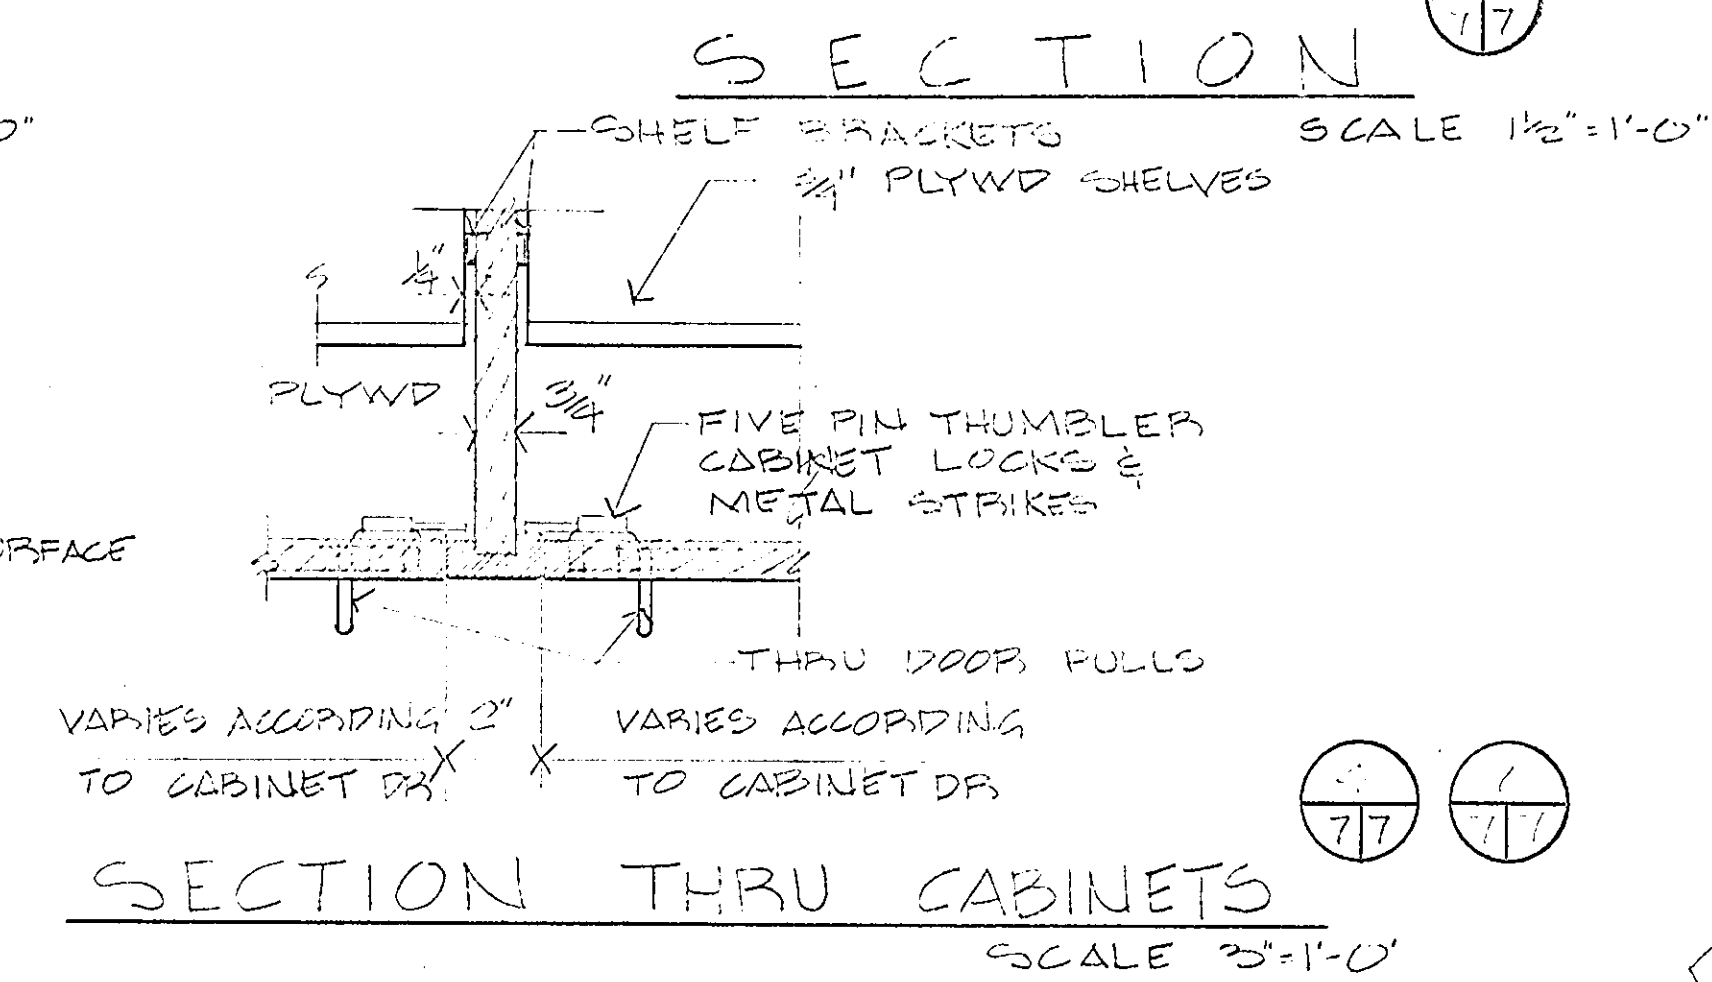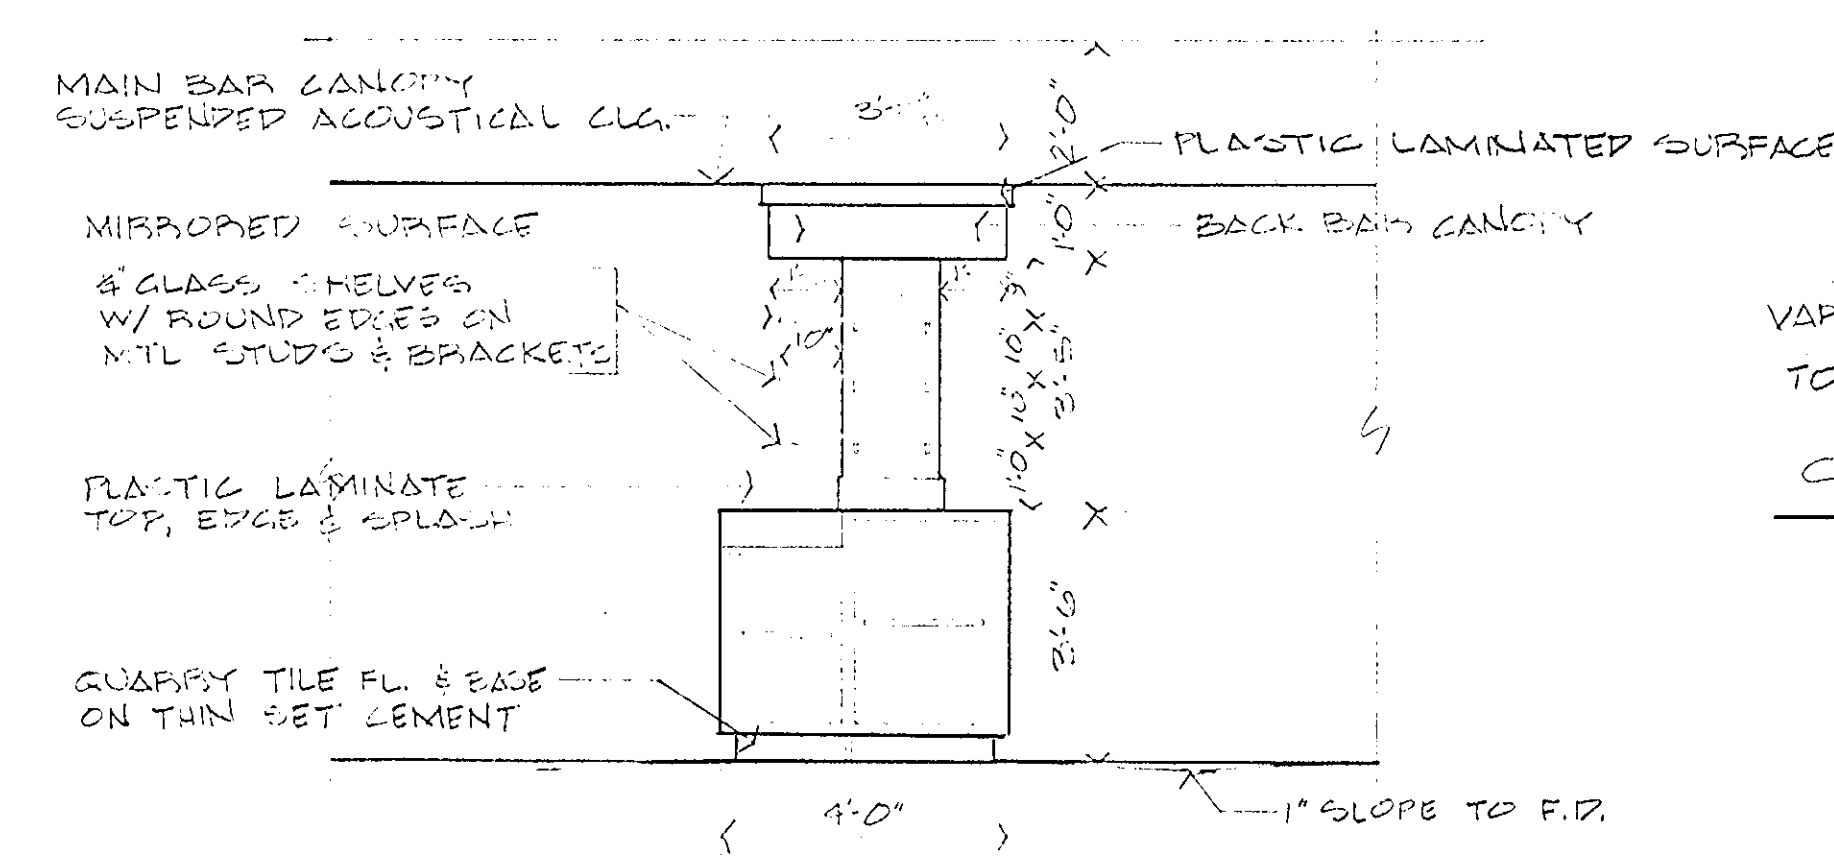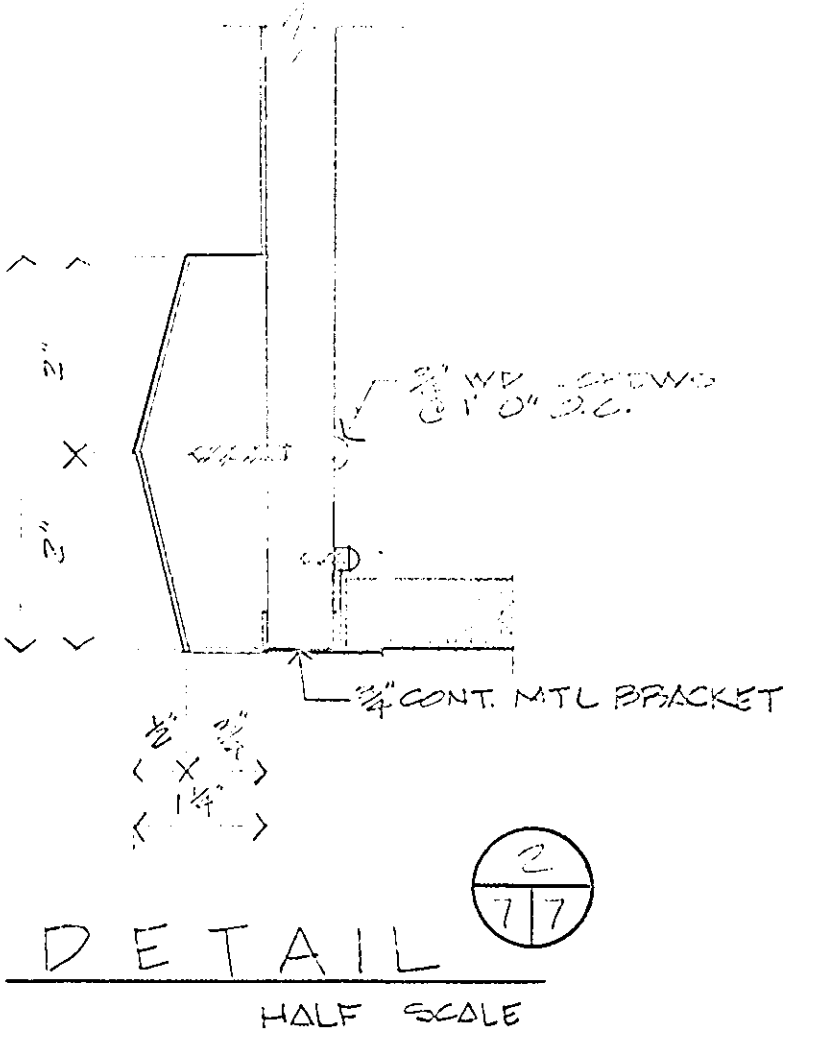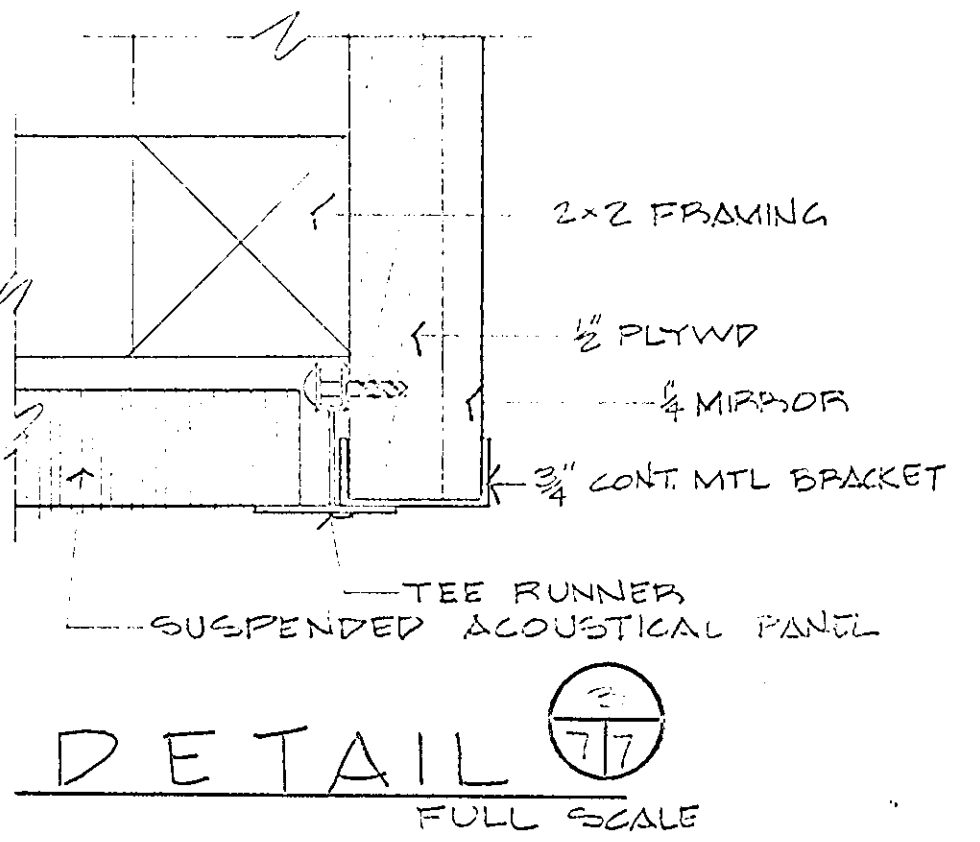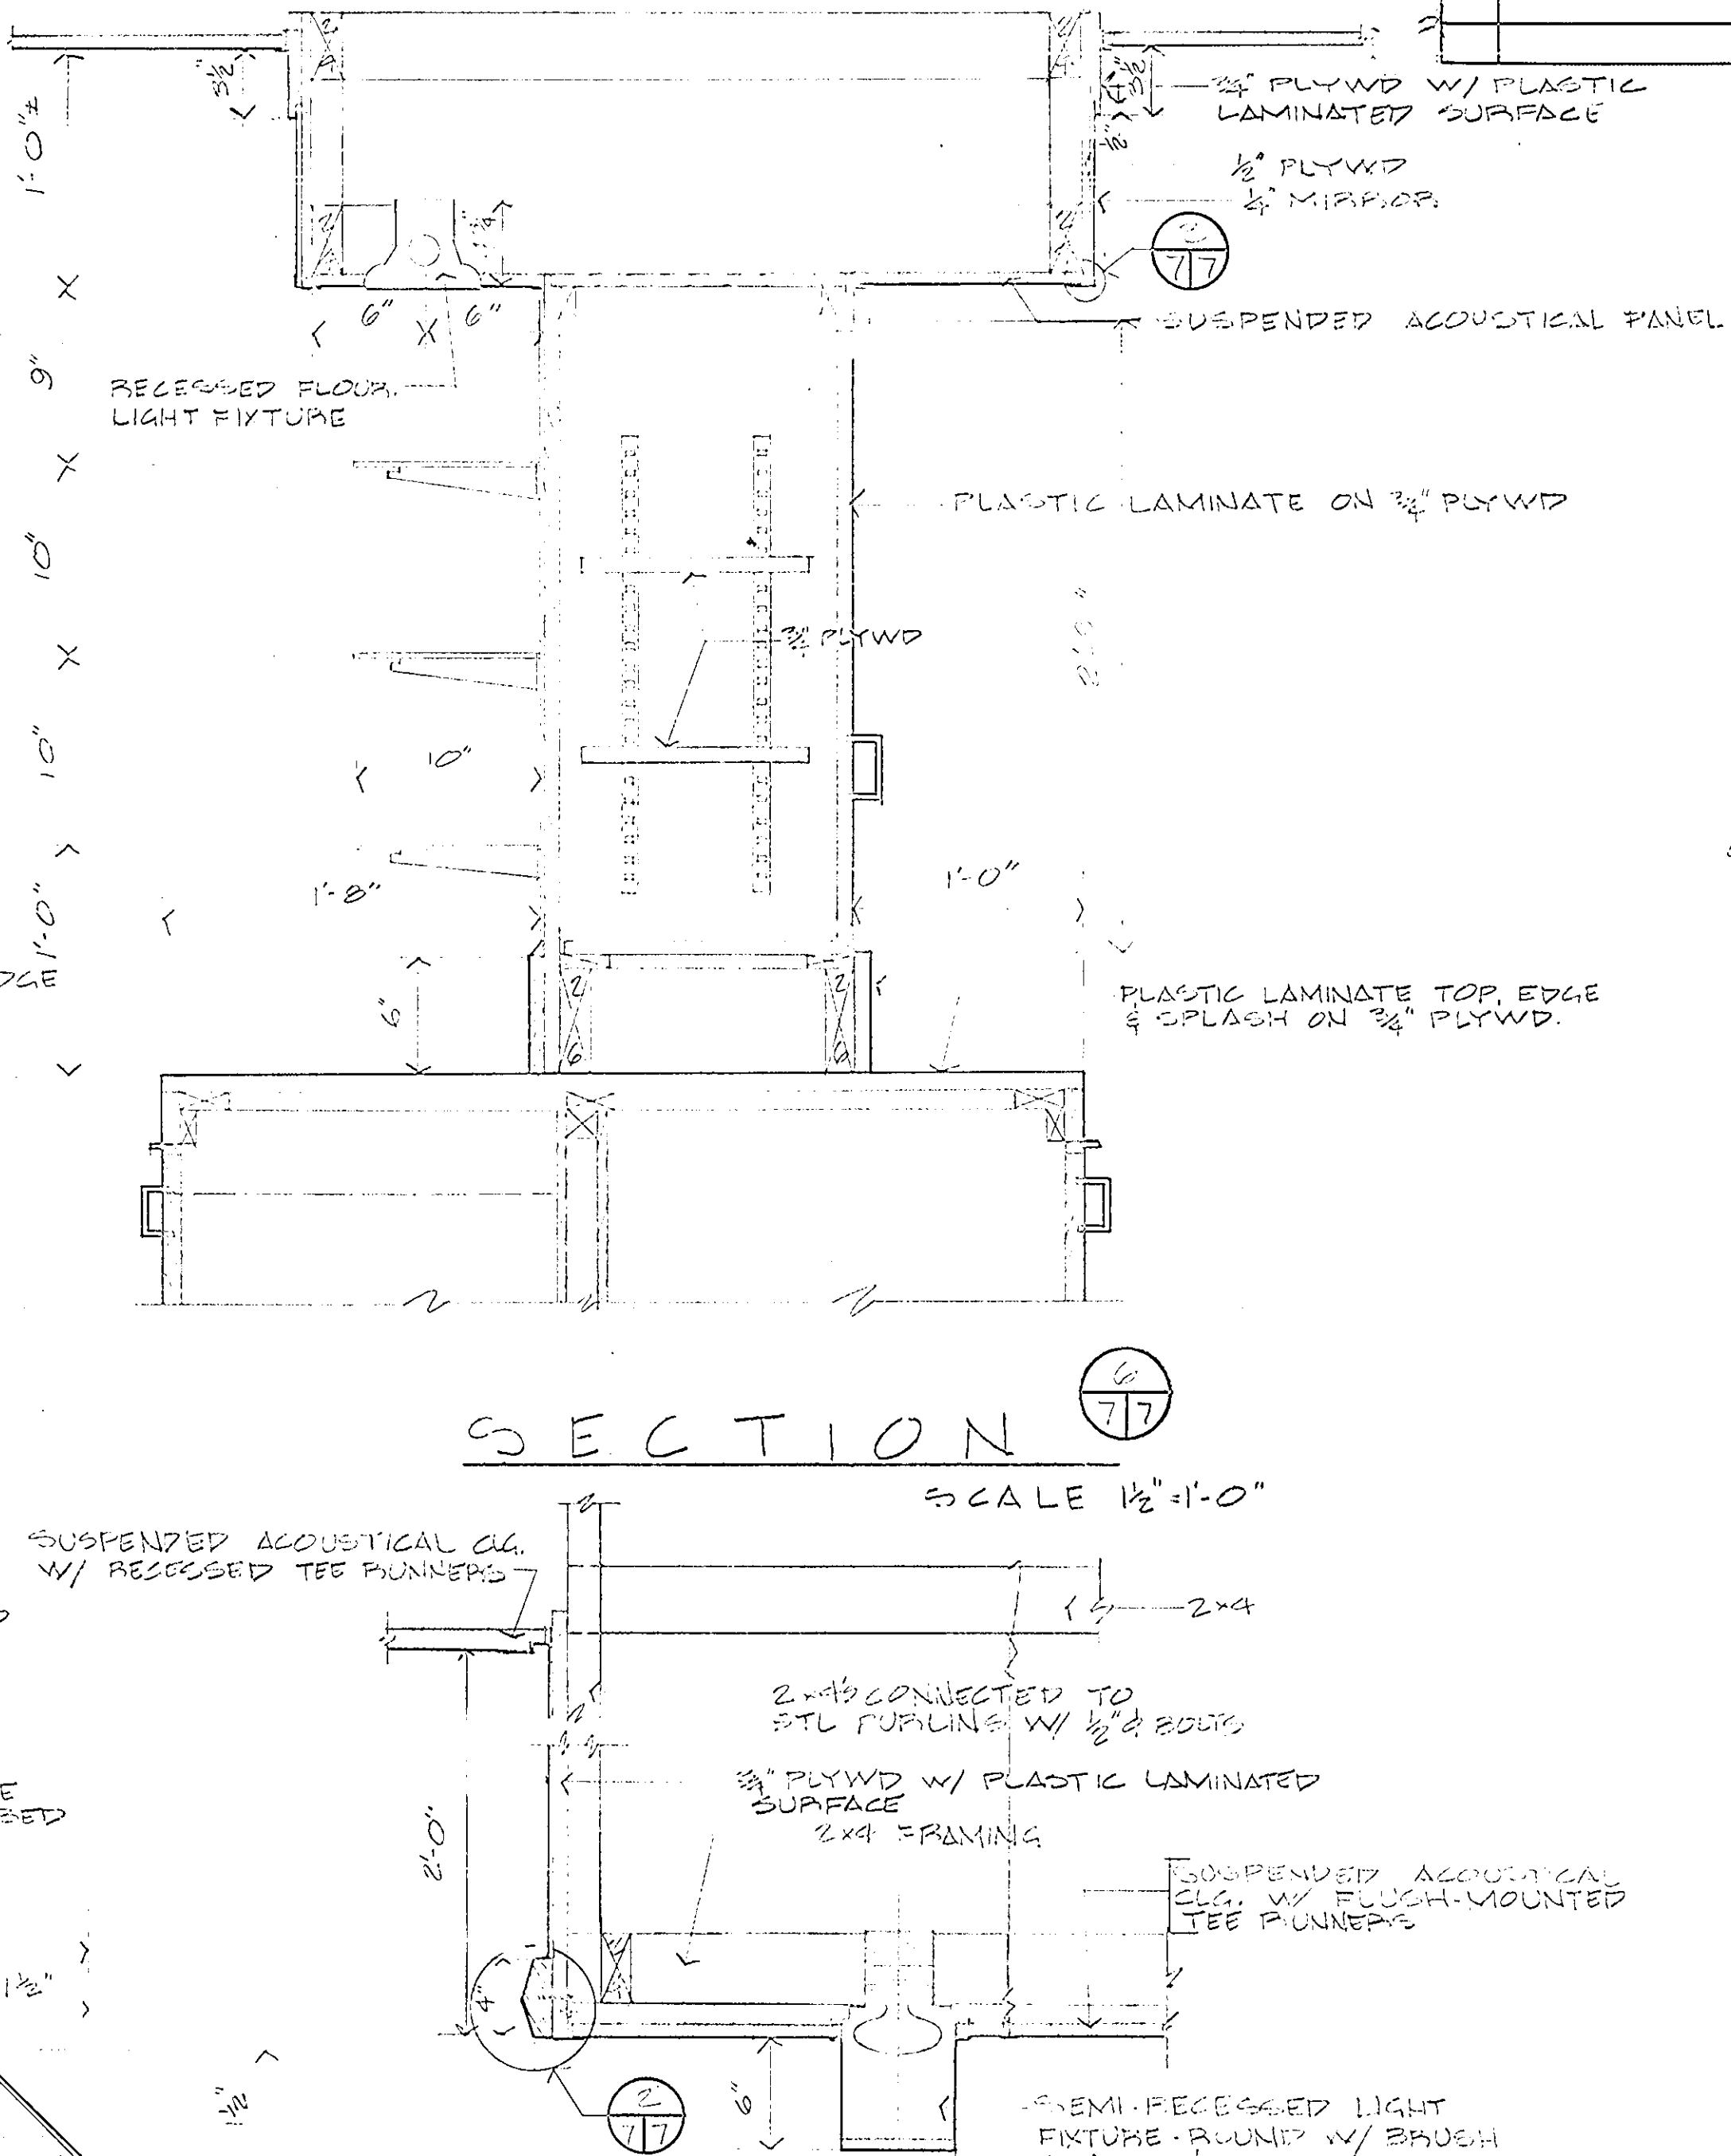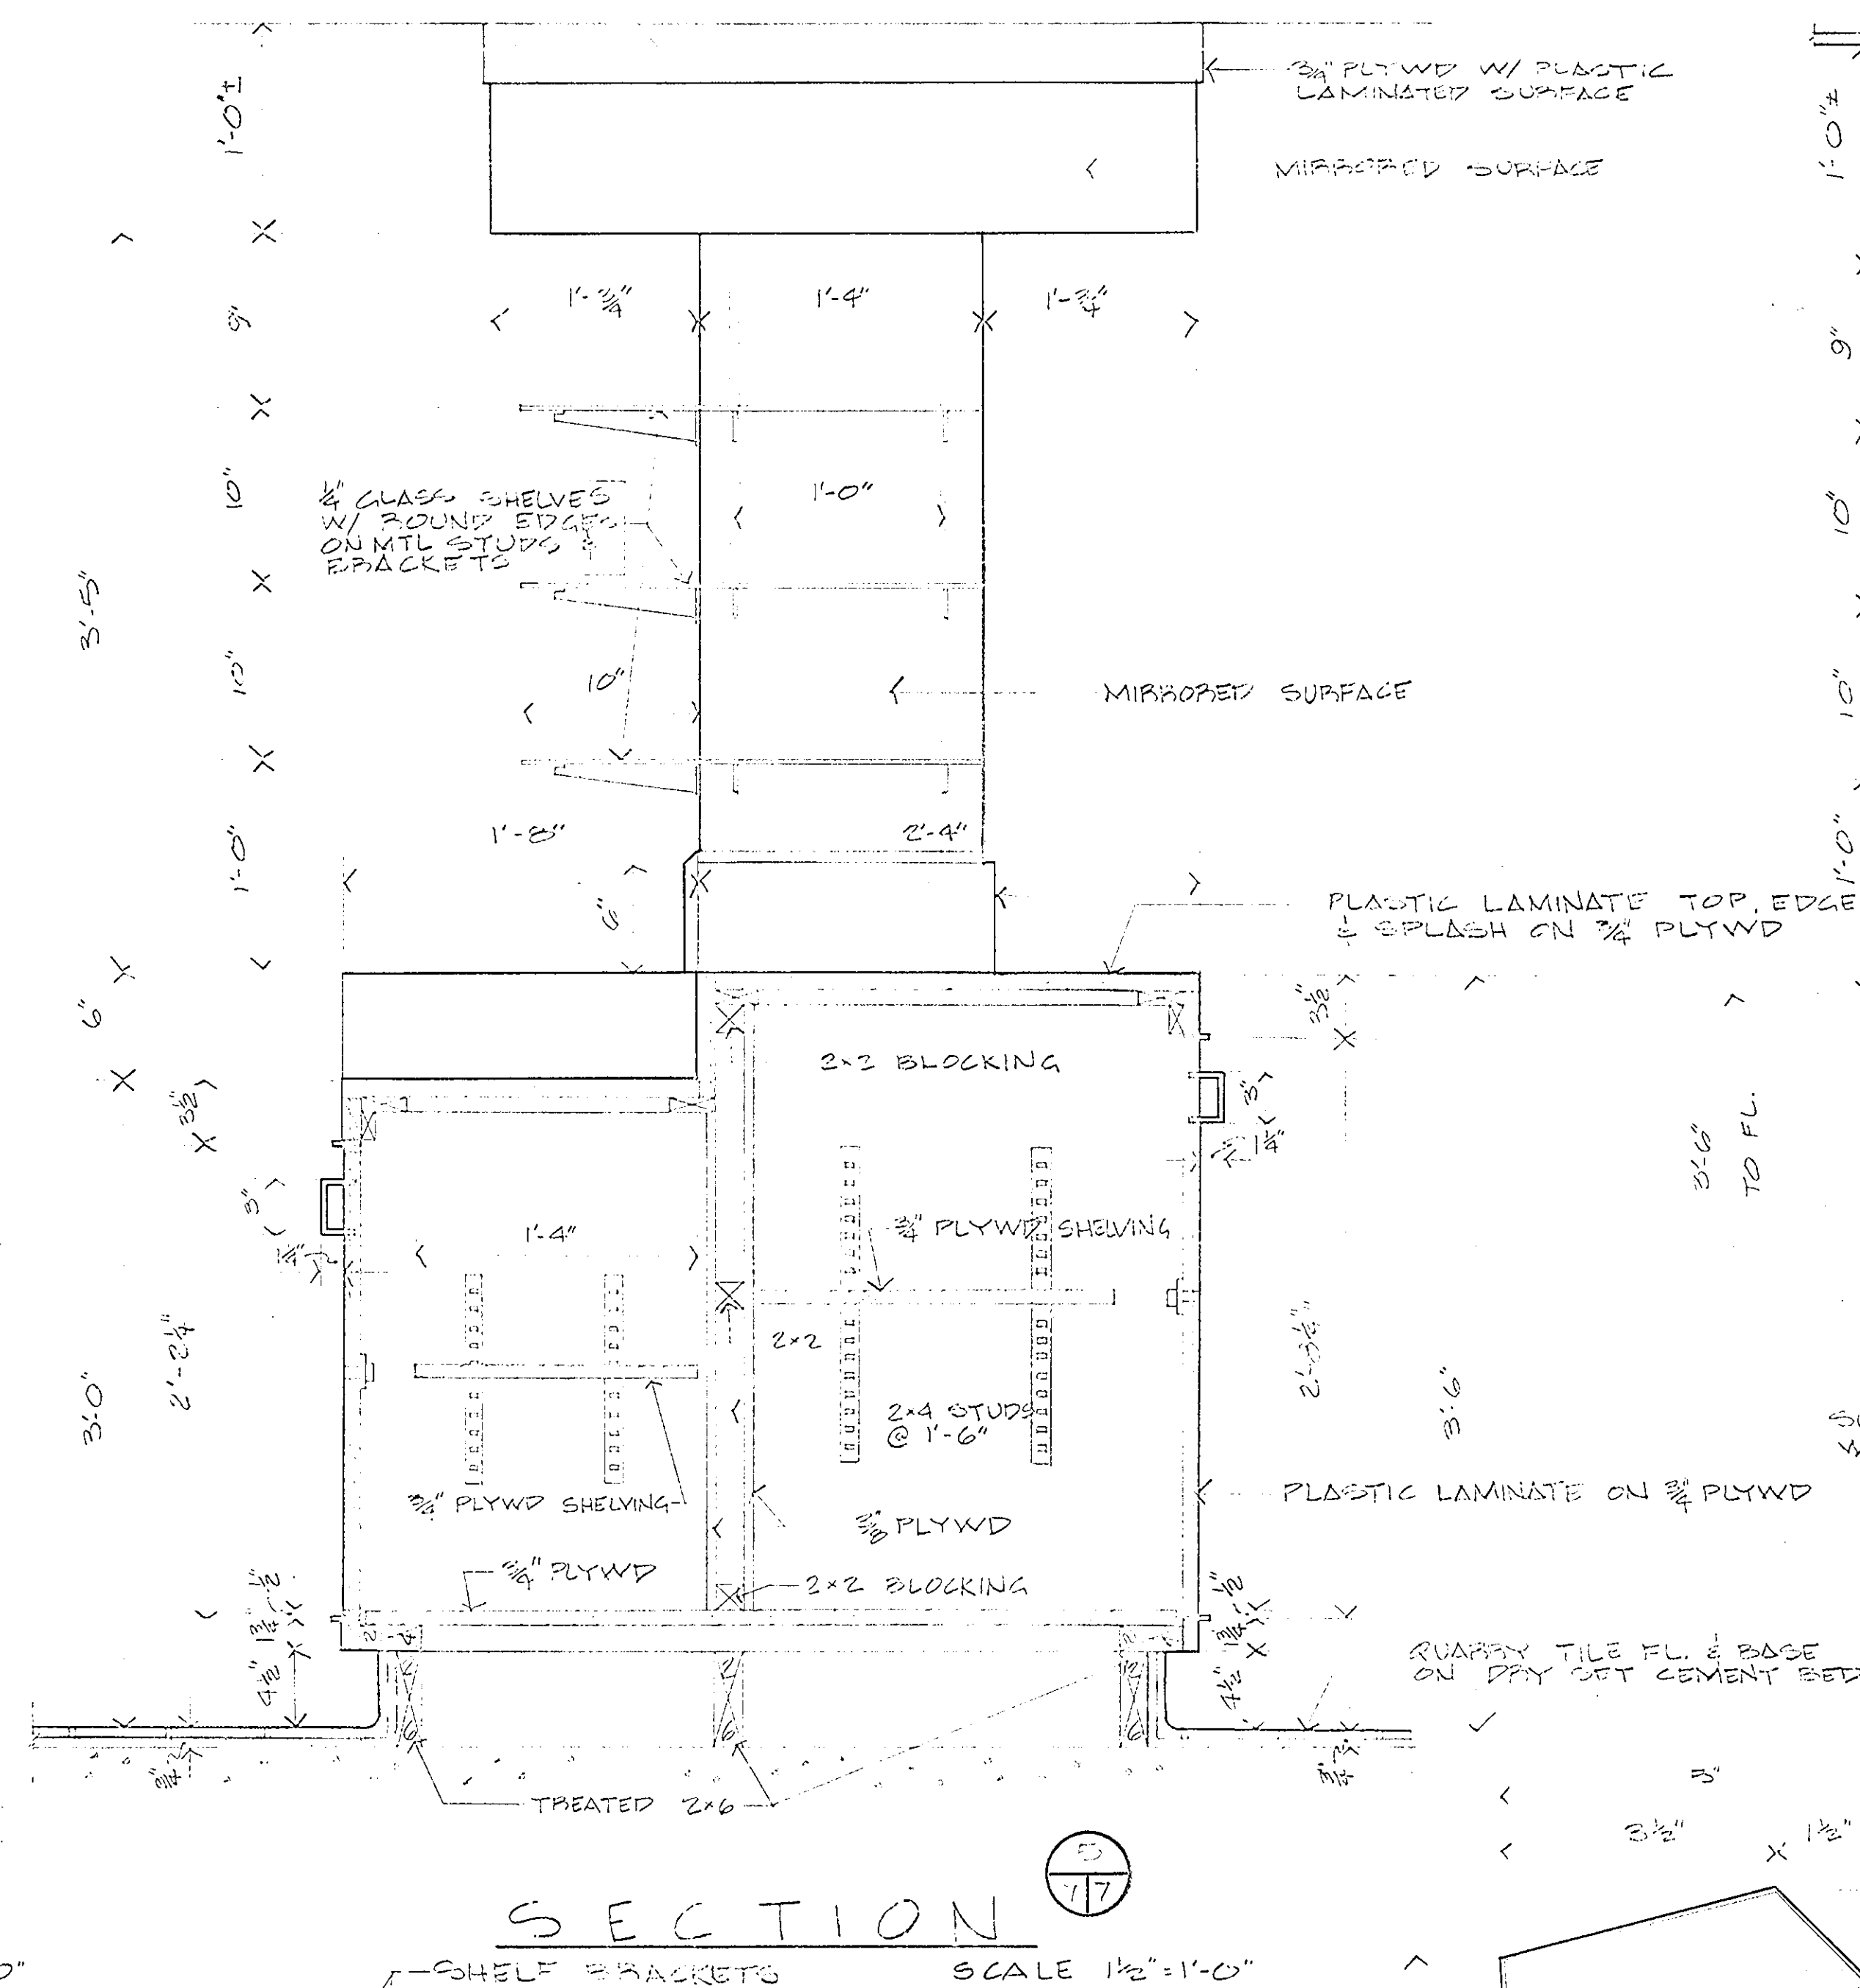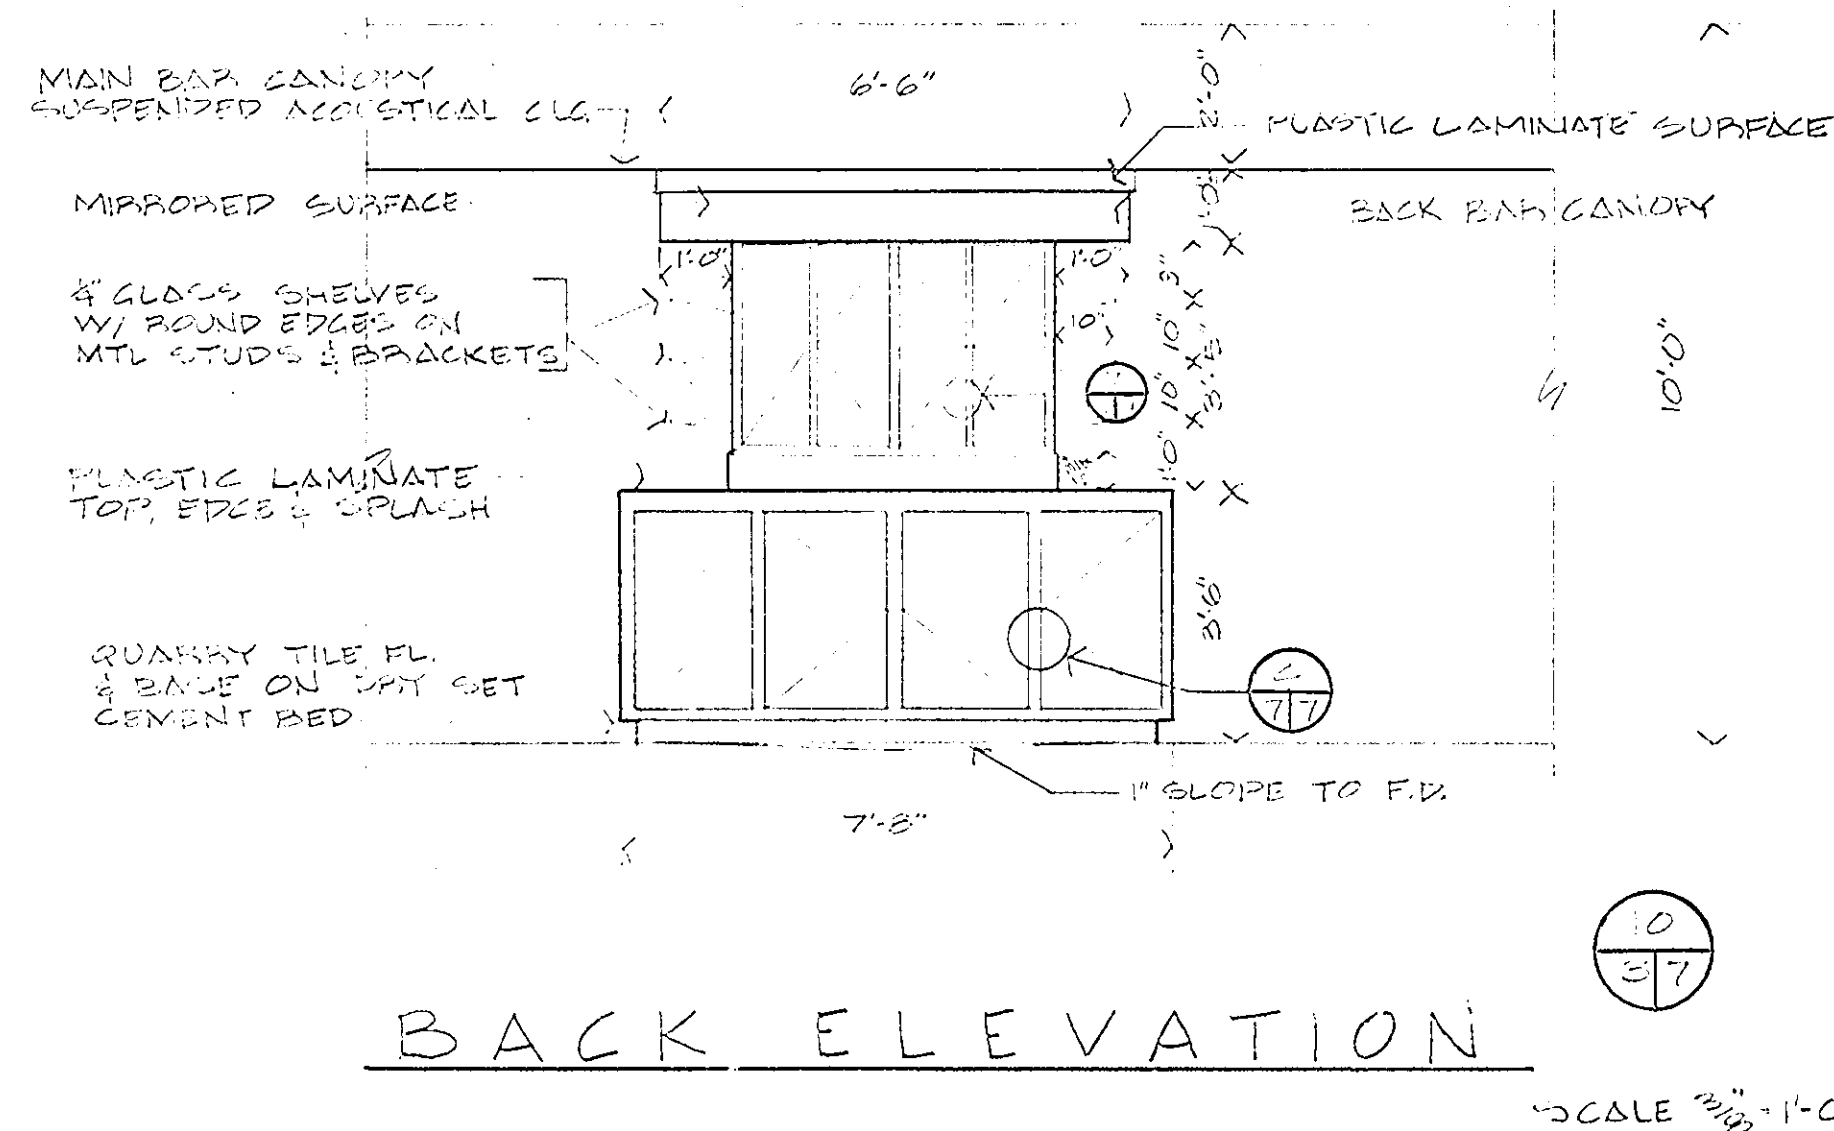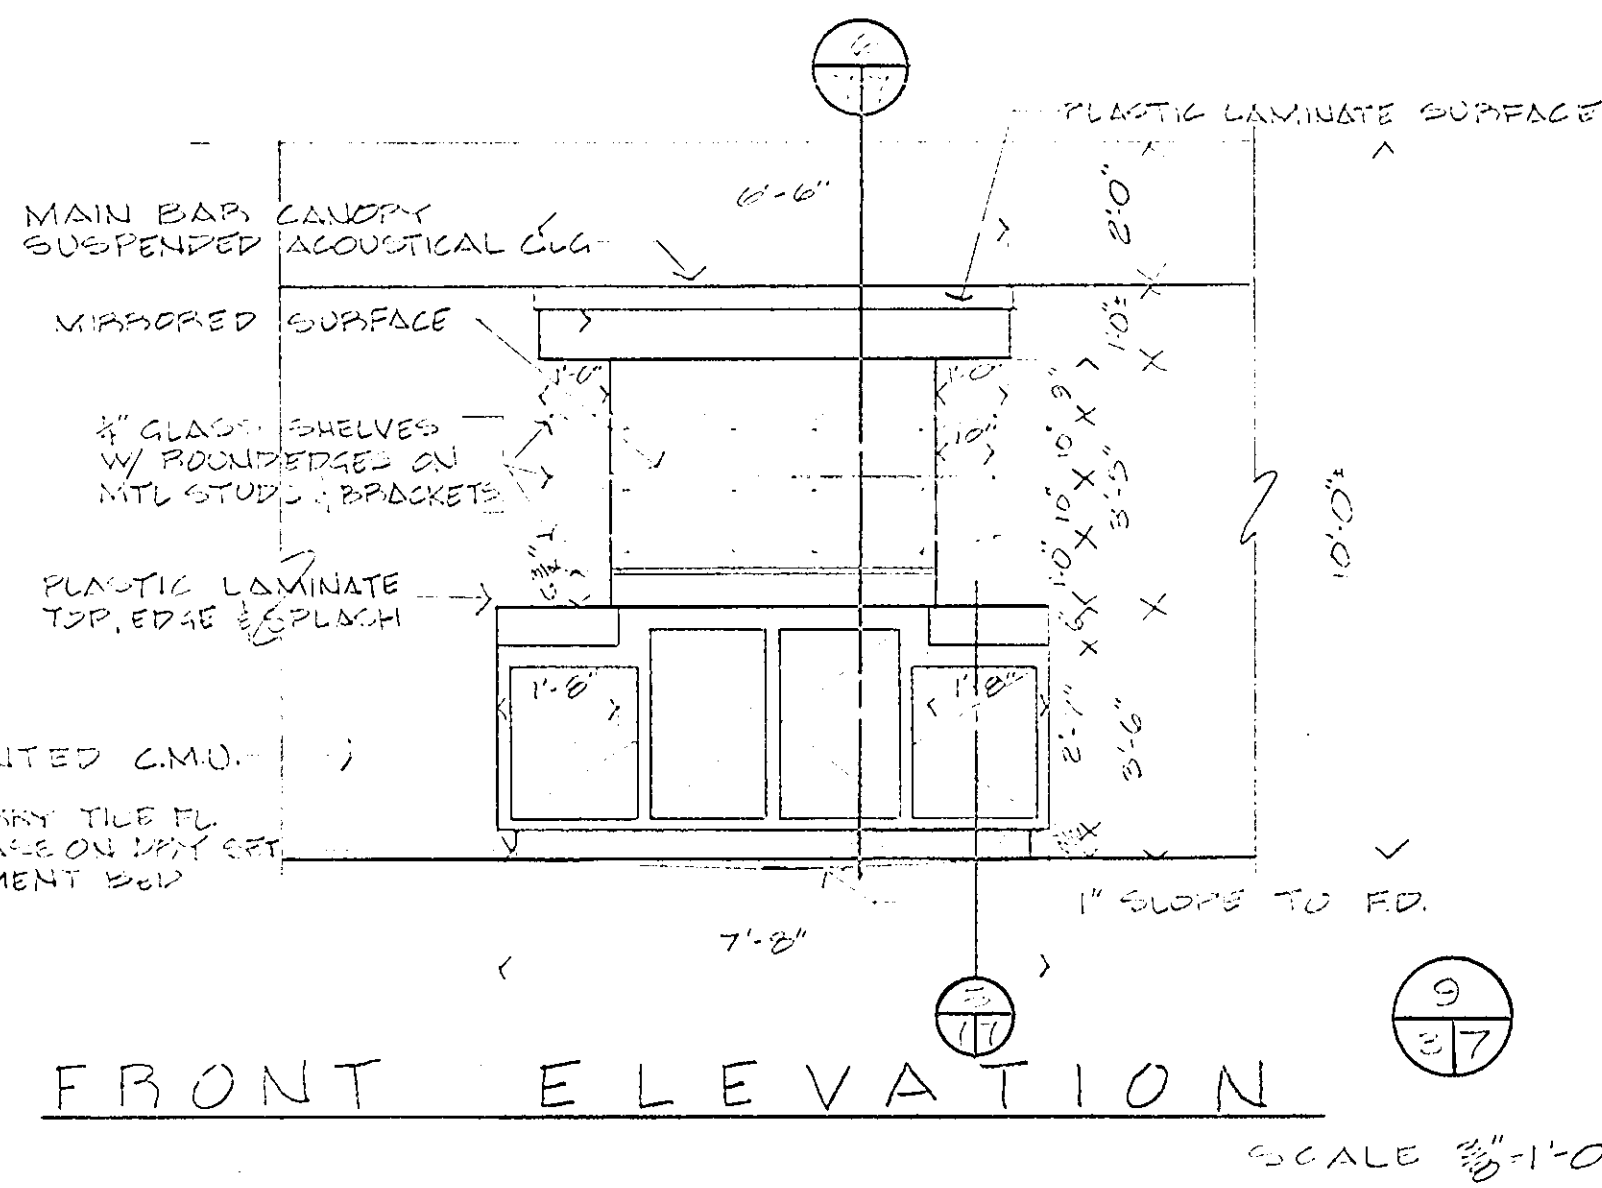

SATISFACTORY TO
DATE 2/26/76


PUBLIC WORKS DEPT. MARINE CORPS BASE CAMP LEJEUNE, N.C.		DEPARTMENT OF THE NAVY NAVAL FACILITIES ENGINEERING COMMAND ATLANTIC DIVISION NORFOLK, VIRGINIA	
DESIGNED BY	CHKD BY	PROJECTED BY	DATE
APPROVED BY	DATE	PUBLIC WORKS OFFICER	DATE
SATISFACTORY TO	DATE	COMMANDING GENERAL	DATE
NO	DIR	DATE	DATE
FOR COMMANDER, NAVFAC			
SIZE	CODE IDENT NO	NAVFAC DRAWING NO	
F	80091	4011890	
SCALE GRAPHIC	SPEC 05-75-0919	CONSTR CONTR NO N62470-75-B-0919	SHEET 7 OF 18
		LANTDIV DWG NO	

REVISIONS			
SYM	DESCRIPTION	DATE	APPROVED

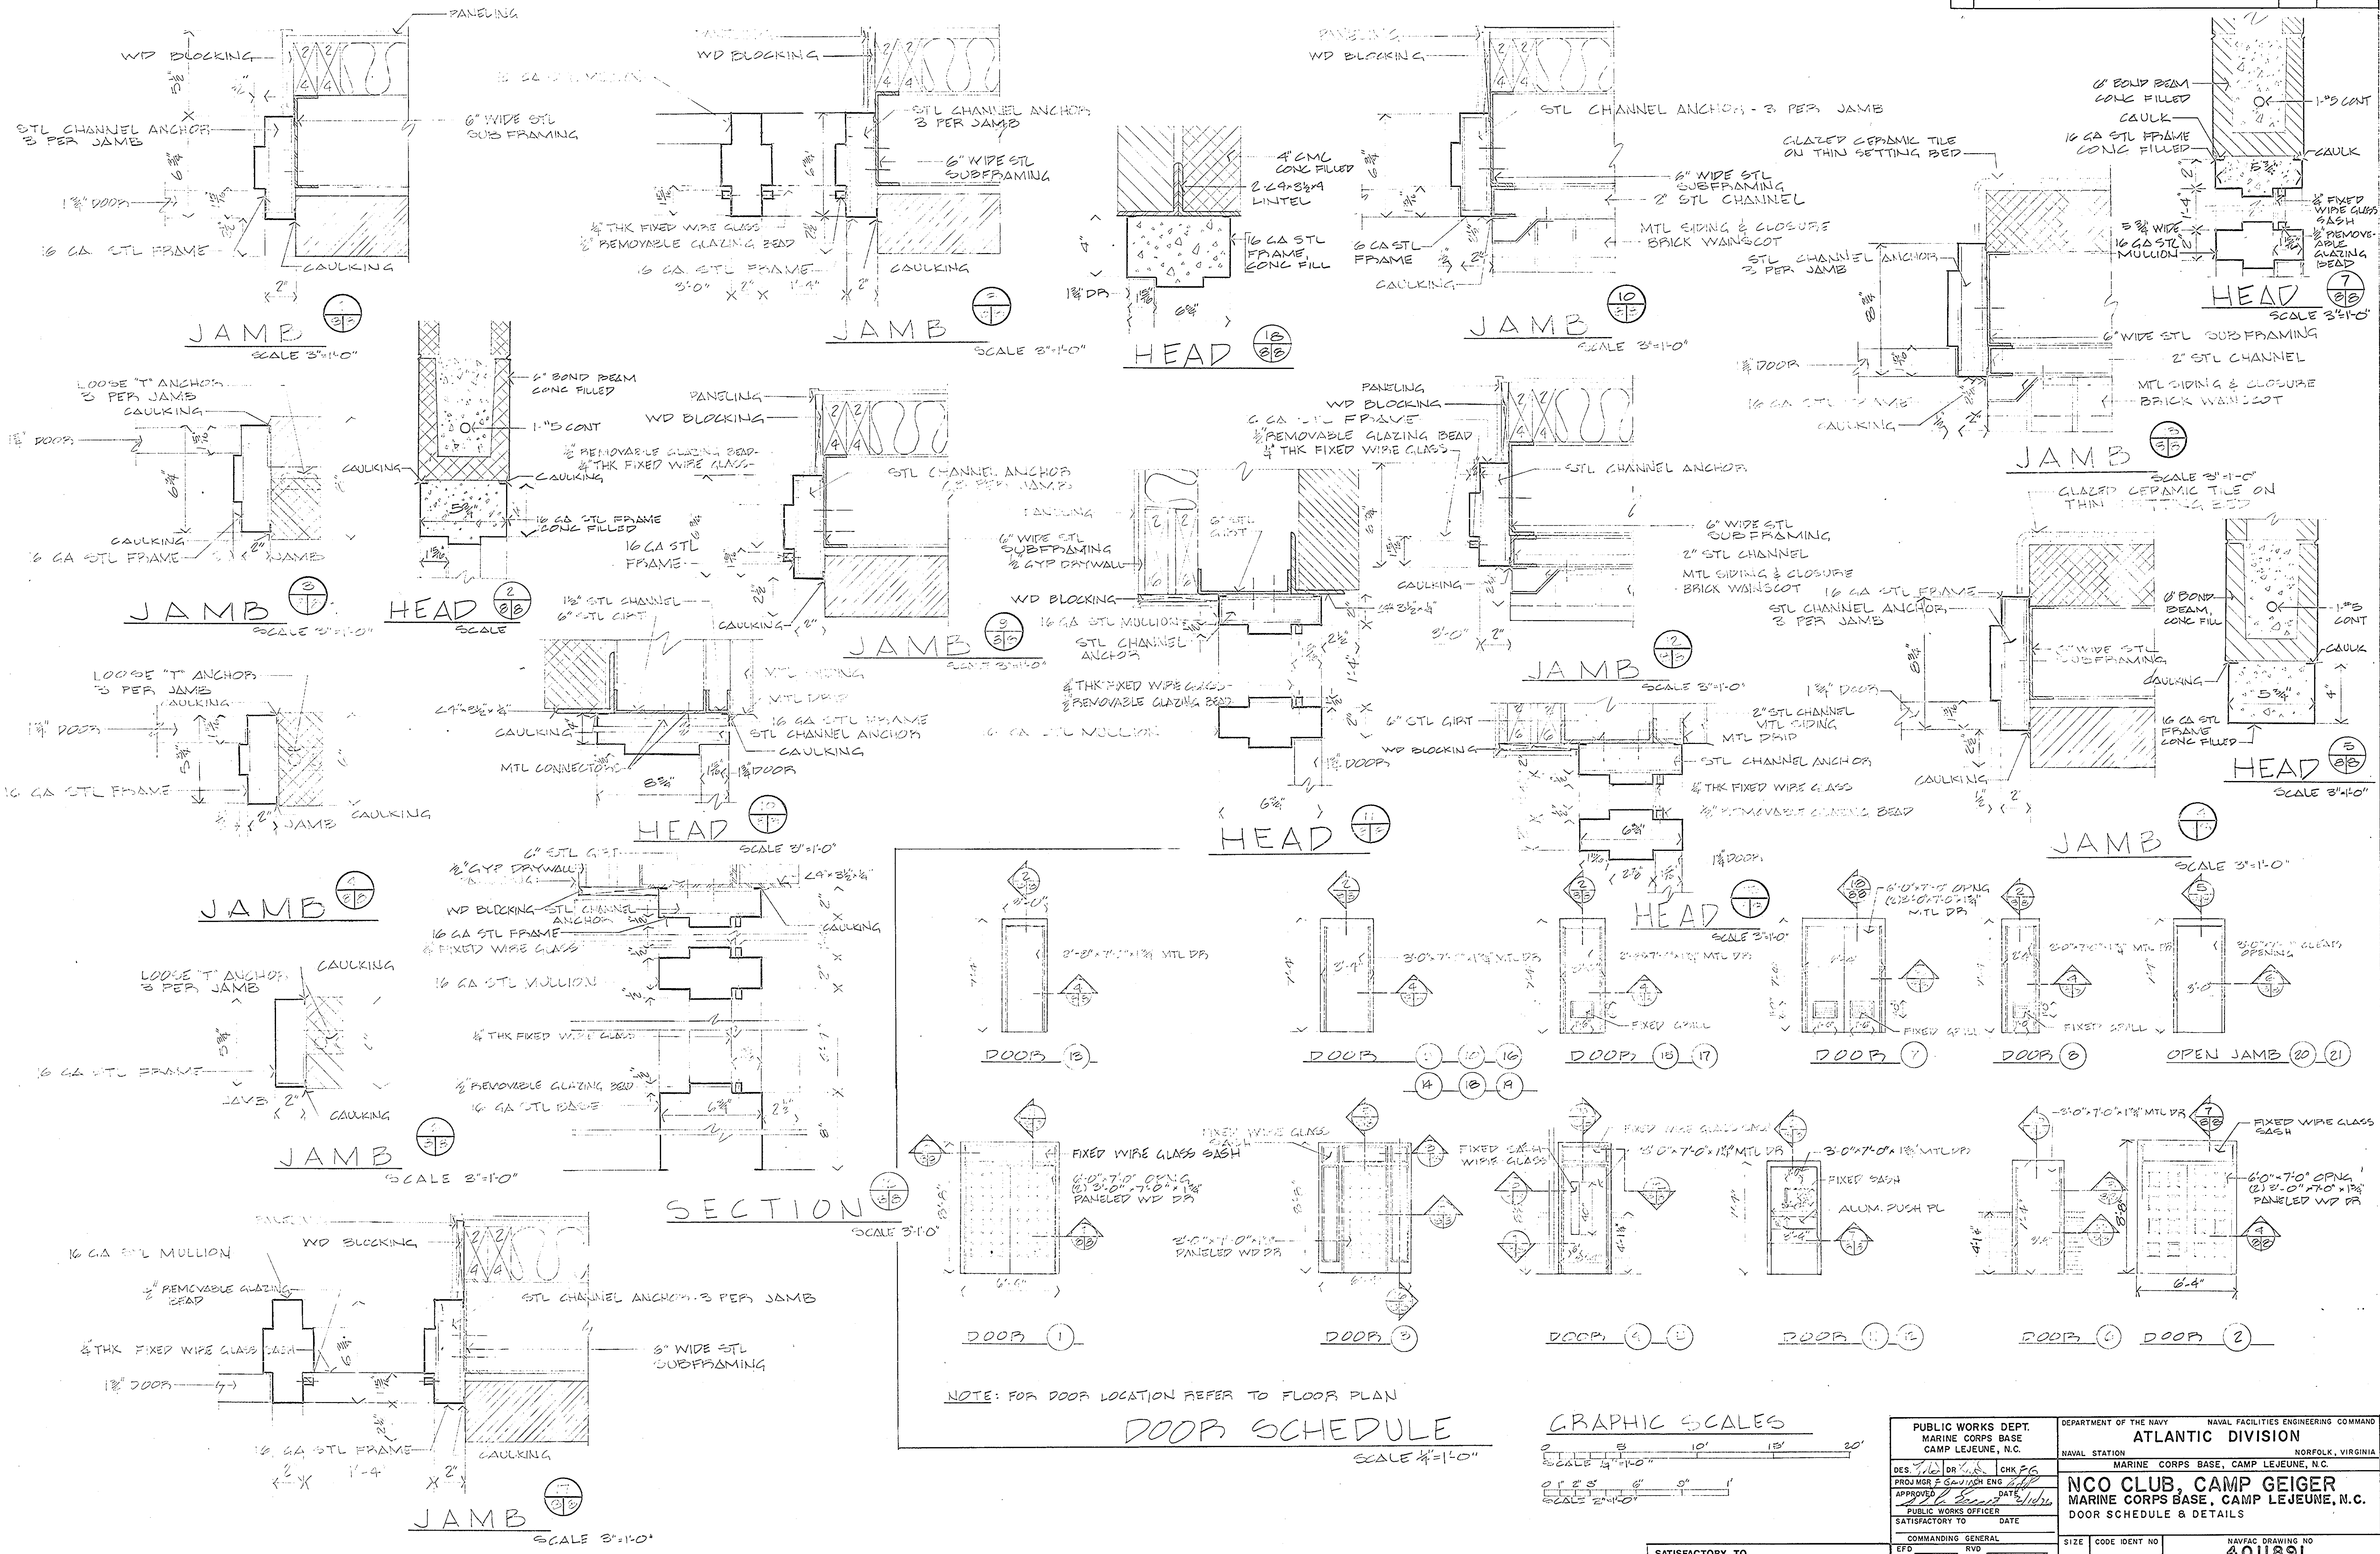


NOTE: FOR DOOR LOCATION REFER TO FLOOR PLAN

DOOR SCHEDULE	
NO.	DESCRIPTION
1	6'-0\"/>
2	6'-0\"/>
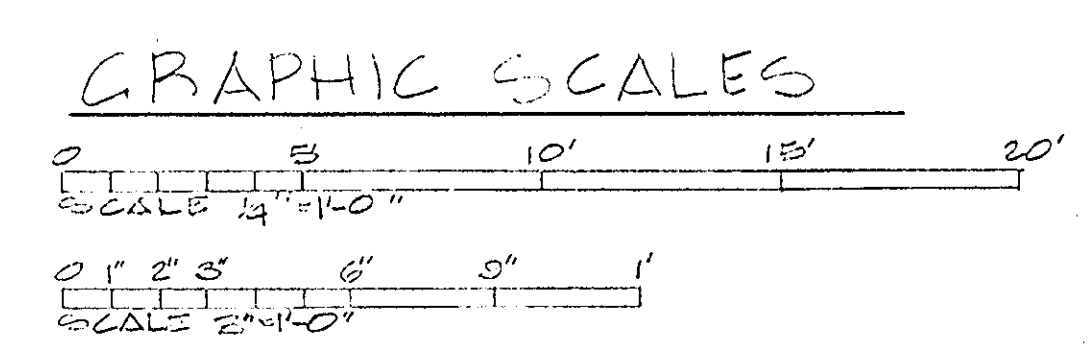




SATISFACTORY TO
[Signature]
 DATE 2/10/76

PUBLIC WORKS DEPT. MARINE CORPS BASE CAMP LEJEUNE, N.C.		DEPARTMENT OF THE NAVY NAVAL FACILITIES ENGINEERING COMMAND ATLANTIC DIVISION NAVAL STATION MARINE CORPS BASE, CAMP LEJEUNE, N.C.	
DES. <i>[Signature]</i>	CHK. <i>[Signature]</i>	NCO CLUB, CAMP GEIGER MARINE CORPS BASE, CAMP LEJEUNE, N.C. DOOR SCHEDULE & DETAILS	
APPROVED <i>[Signature]</i>	DATE <i>[Signature]</i>	SIZE F	CODE IDENT NO 80091
SATISFACTORY TO	DATE	NAVJAG DRAWING NO 4011891	CONSTR CONTR NO N62470-75-B-0919
COMMANDING GENERAL		SHEET 8 OF 18	
EFD	RVD	LANTOIN DVG NO	
ND	DIR		
APPROVED <i>[Signature]</i>			
DATE <i>[Signature]</i>			
FOR COMMANDER, NAVJAG			



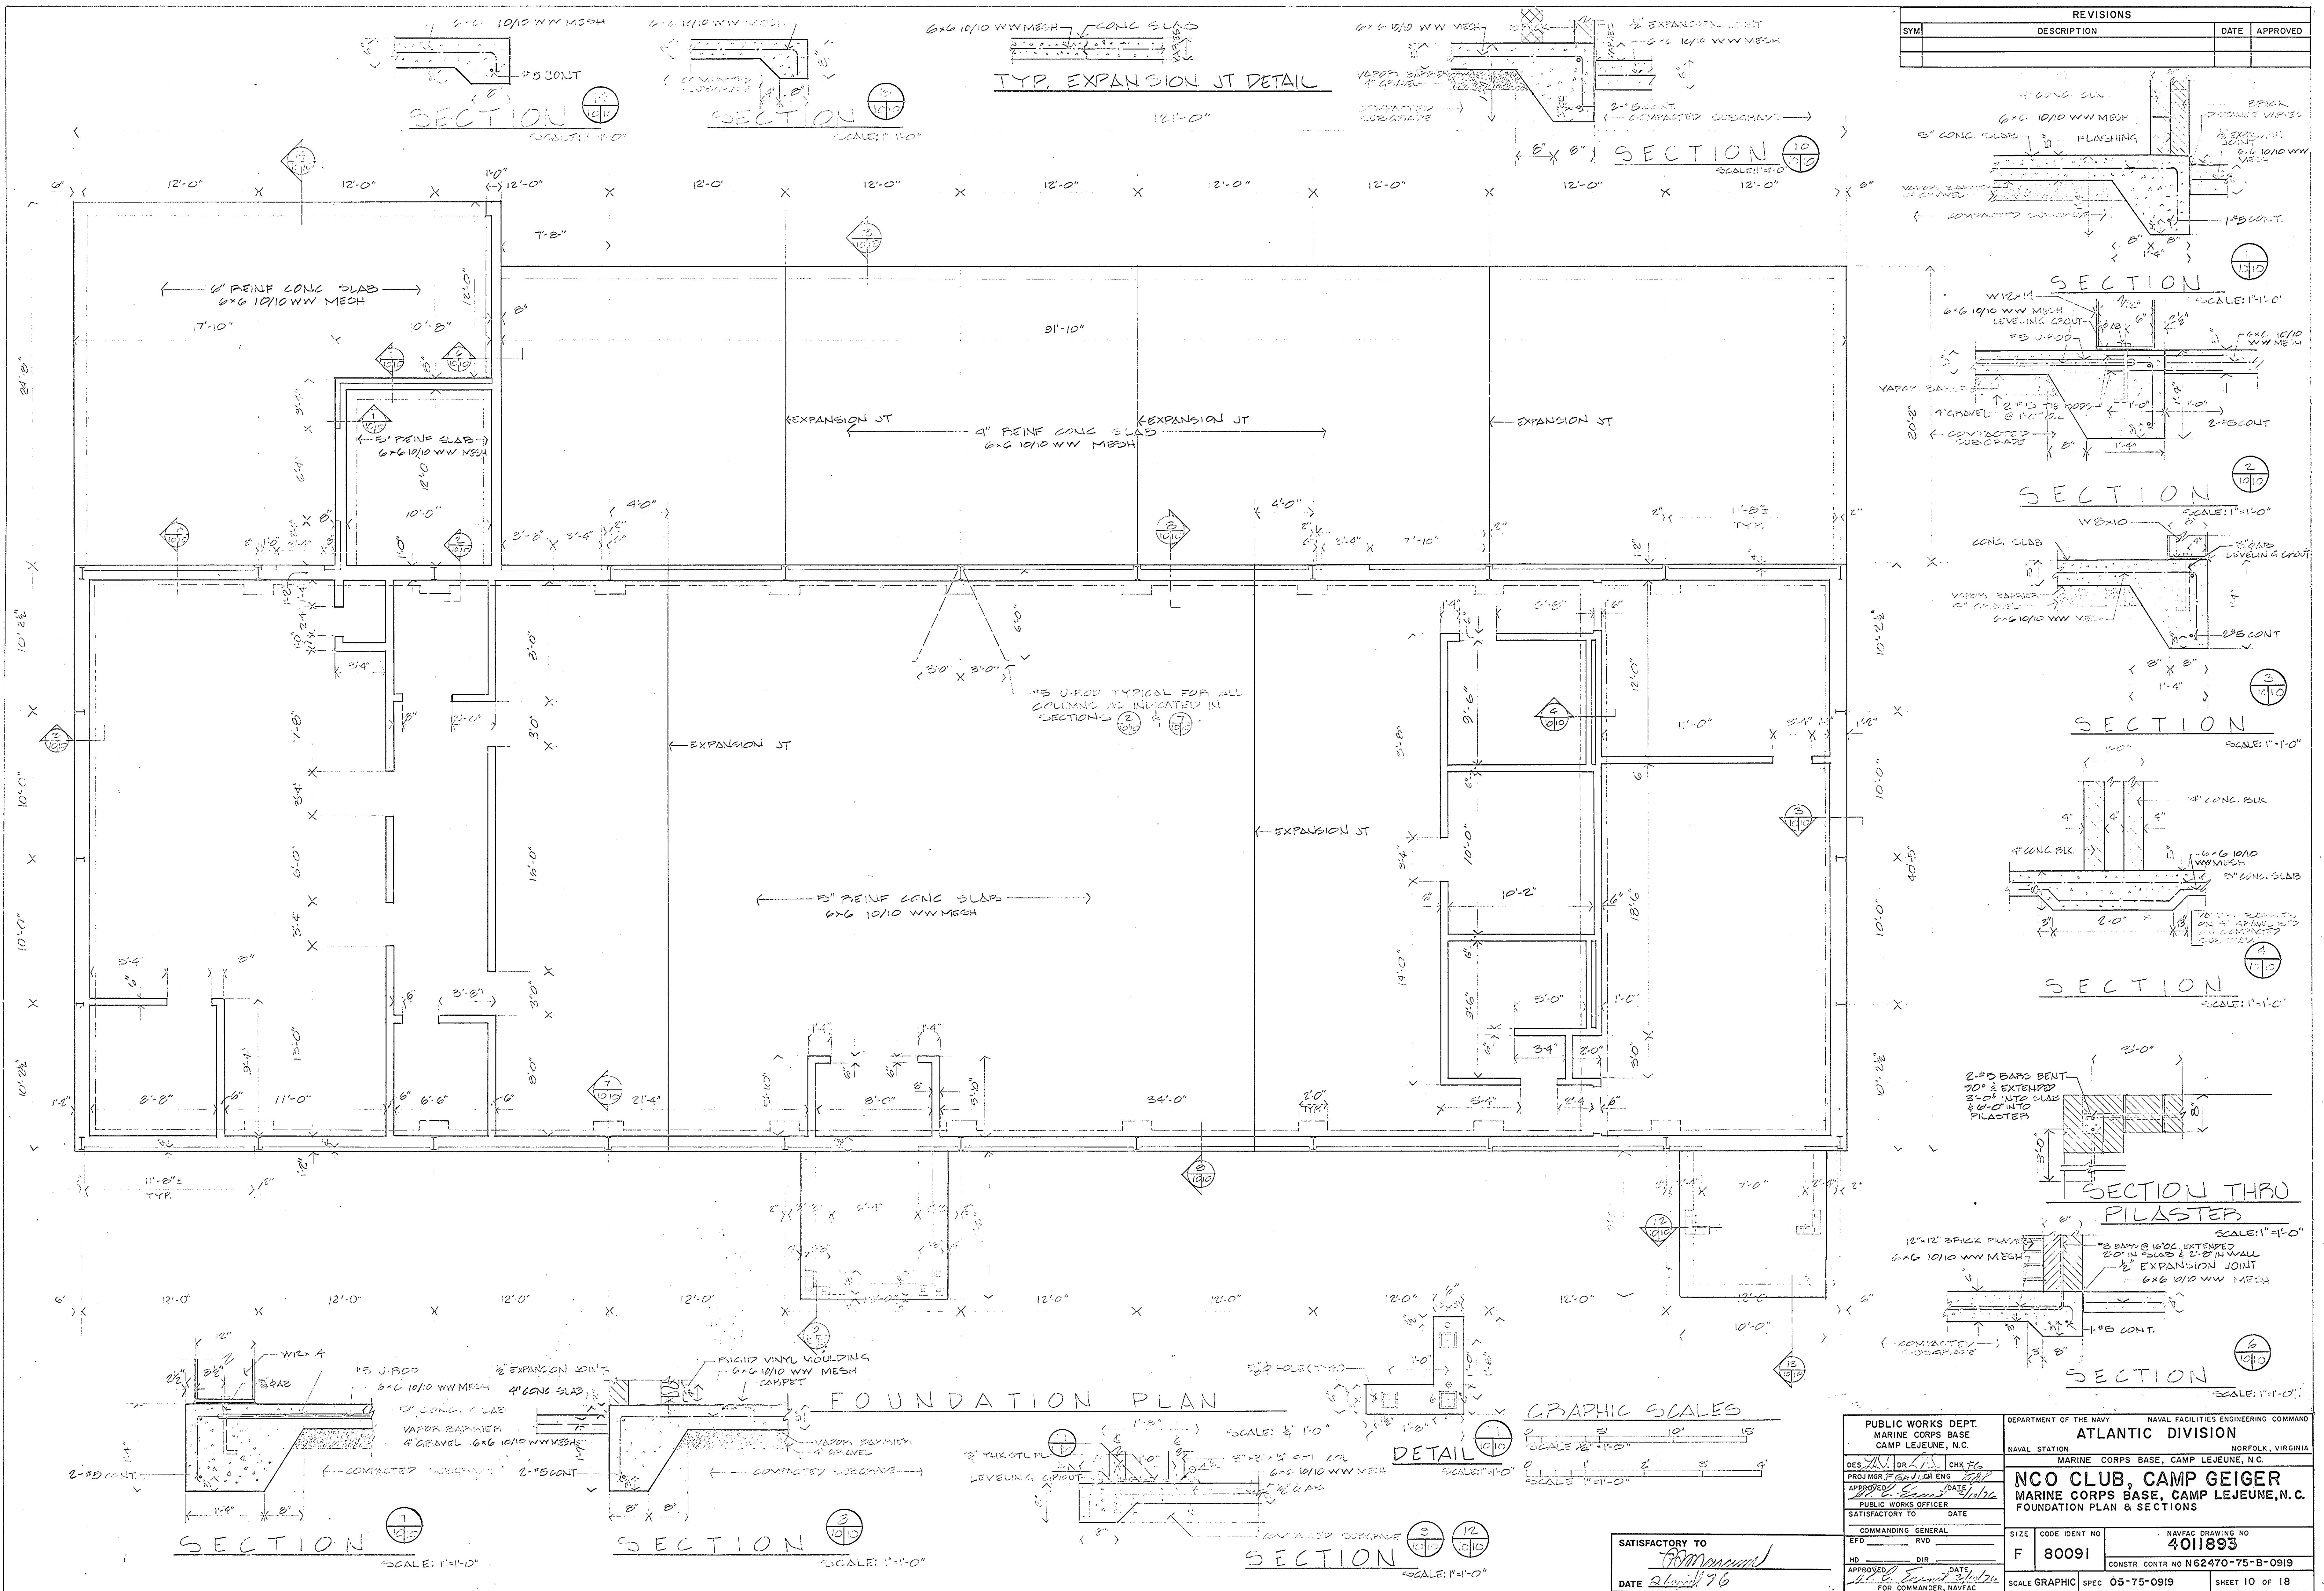


REVISIONS			
SYM	DESCRIPTION	DATE	APPROVED

PUBLIC WORKS DEPT. MARINE CORPS BASE CAMP LEJEUNE, N.C.		DEPARTMENT OF THE NAVY NAVAL FACILITIES ENGINEERING COMMAND ATLANTIC DIVISION	
DES. <i>[Signature]</i> DR. <i>[Signature]</i> CHK. <i>[Signature]</i>		MARINE CORPS BASE, CAMP LEJEUNE, N.C.	
PROJ. MGR. <i>[Signature]</i> CIV. ENGR. <i>[Signature]</i>		NCO CLUB, CAMP GEIGER MARINE CORPS BASE, CAMP LEJEUNE, N.C.	
APPROVED <i>[Signature]</i> DATE <i>[Date]</i>		FOUNDATION PLAN & SECTIONS	
PUBLIC WORKS OFFICER		NAVFAC DRAWING NO. 4011893	
SATISFACTORY TO		SIZE CODE IDENT NO. 80091	
COMMANDING GENERAL		CONSTR. CONTR. NO. N62470-75-B-0919	
EFD <i>[Signature]</i> RVD <i>[Signature]</i>		SCALE GRAPHIC SPEC 05-75-0919	
HD <i>[Signature]</i> DIR <i>[Signature]</i>		SHEET 10 OF 18	
APPROVED <i>[Signature]</i> DATE <i>[Date]</i>		LANTDIV DWS NO.	
FOR COMMANDER, NAVFAC			

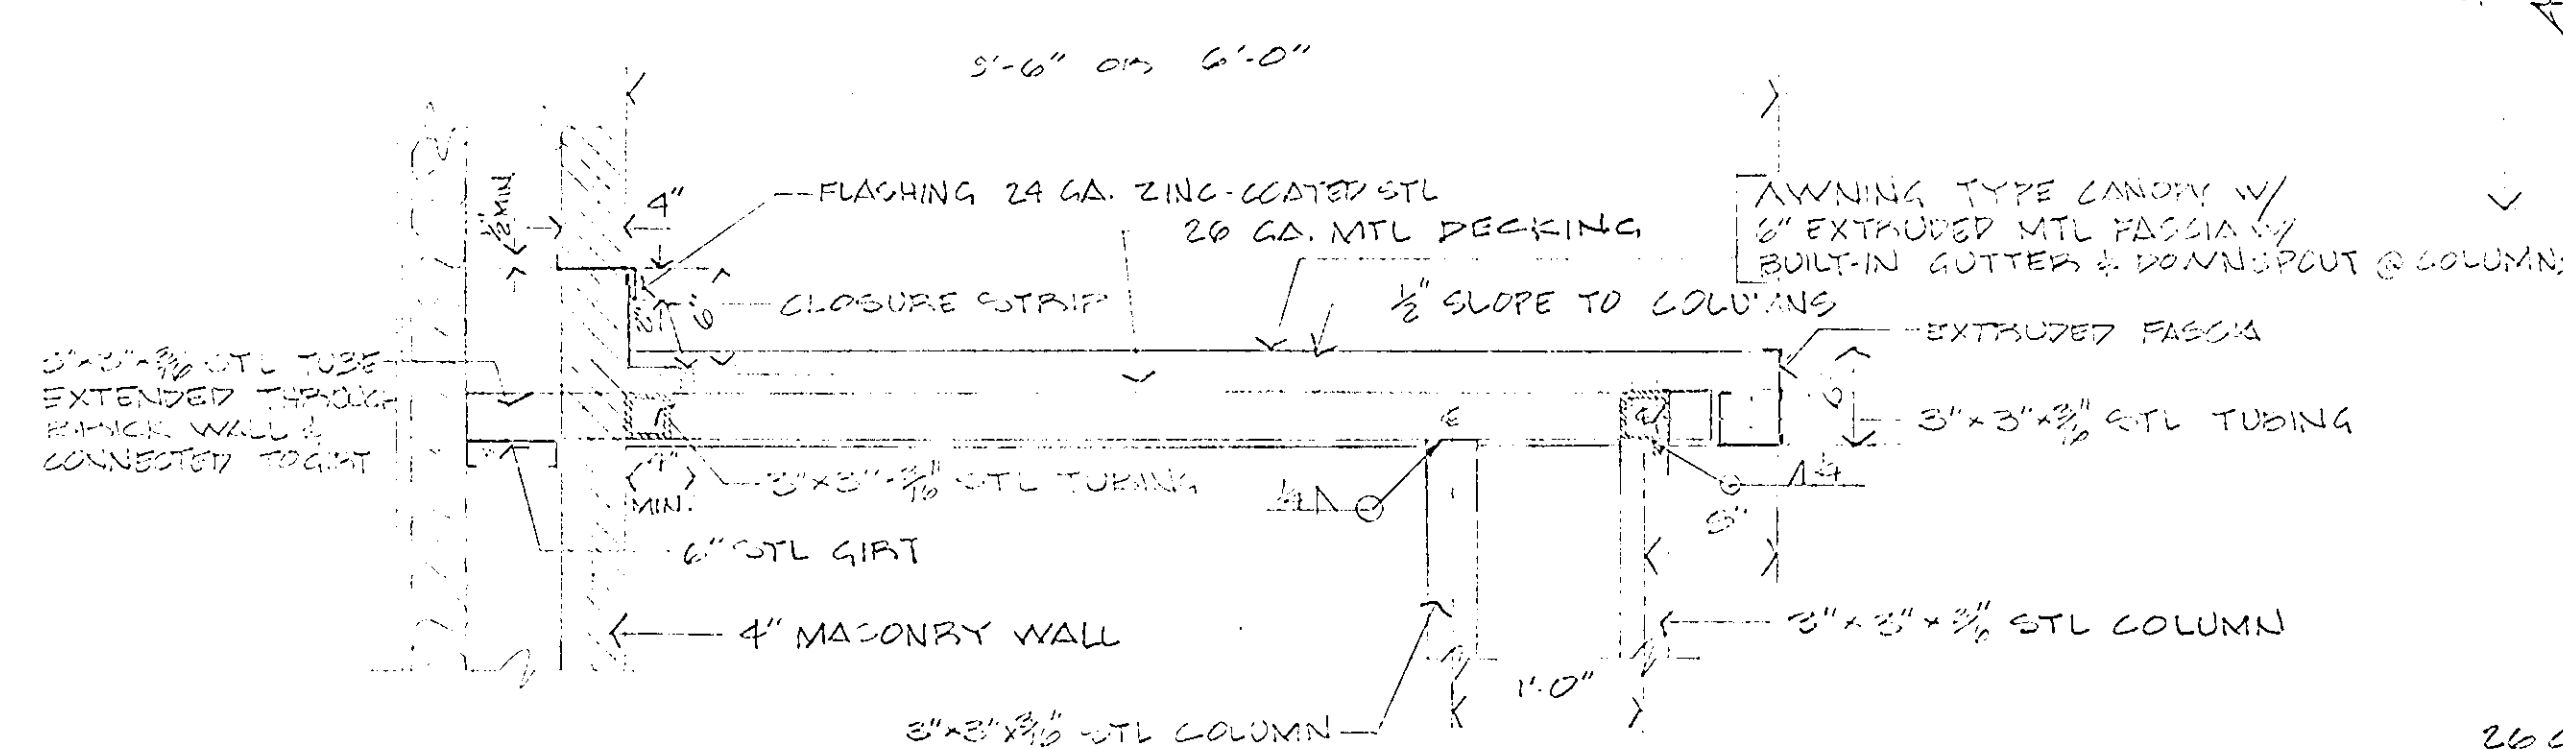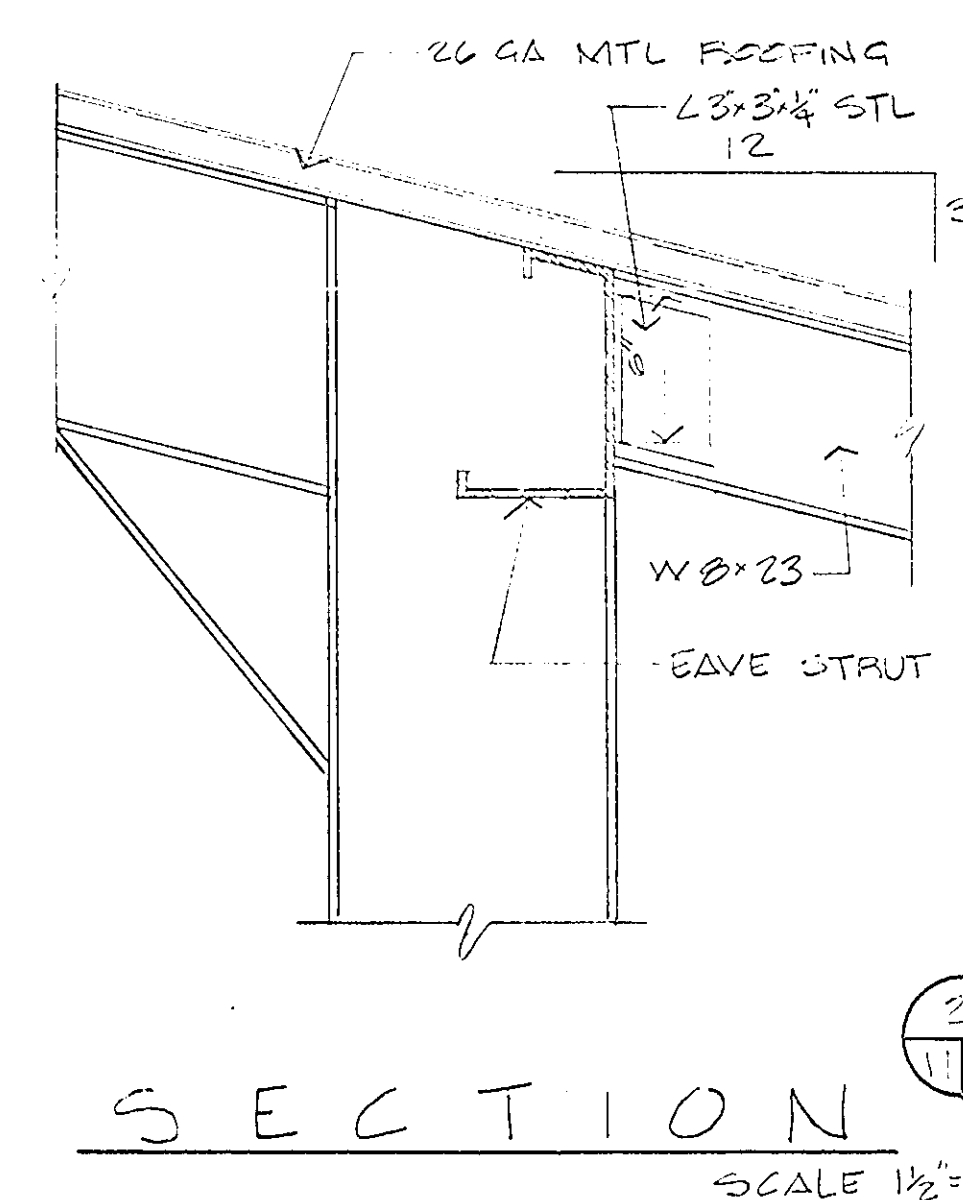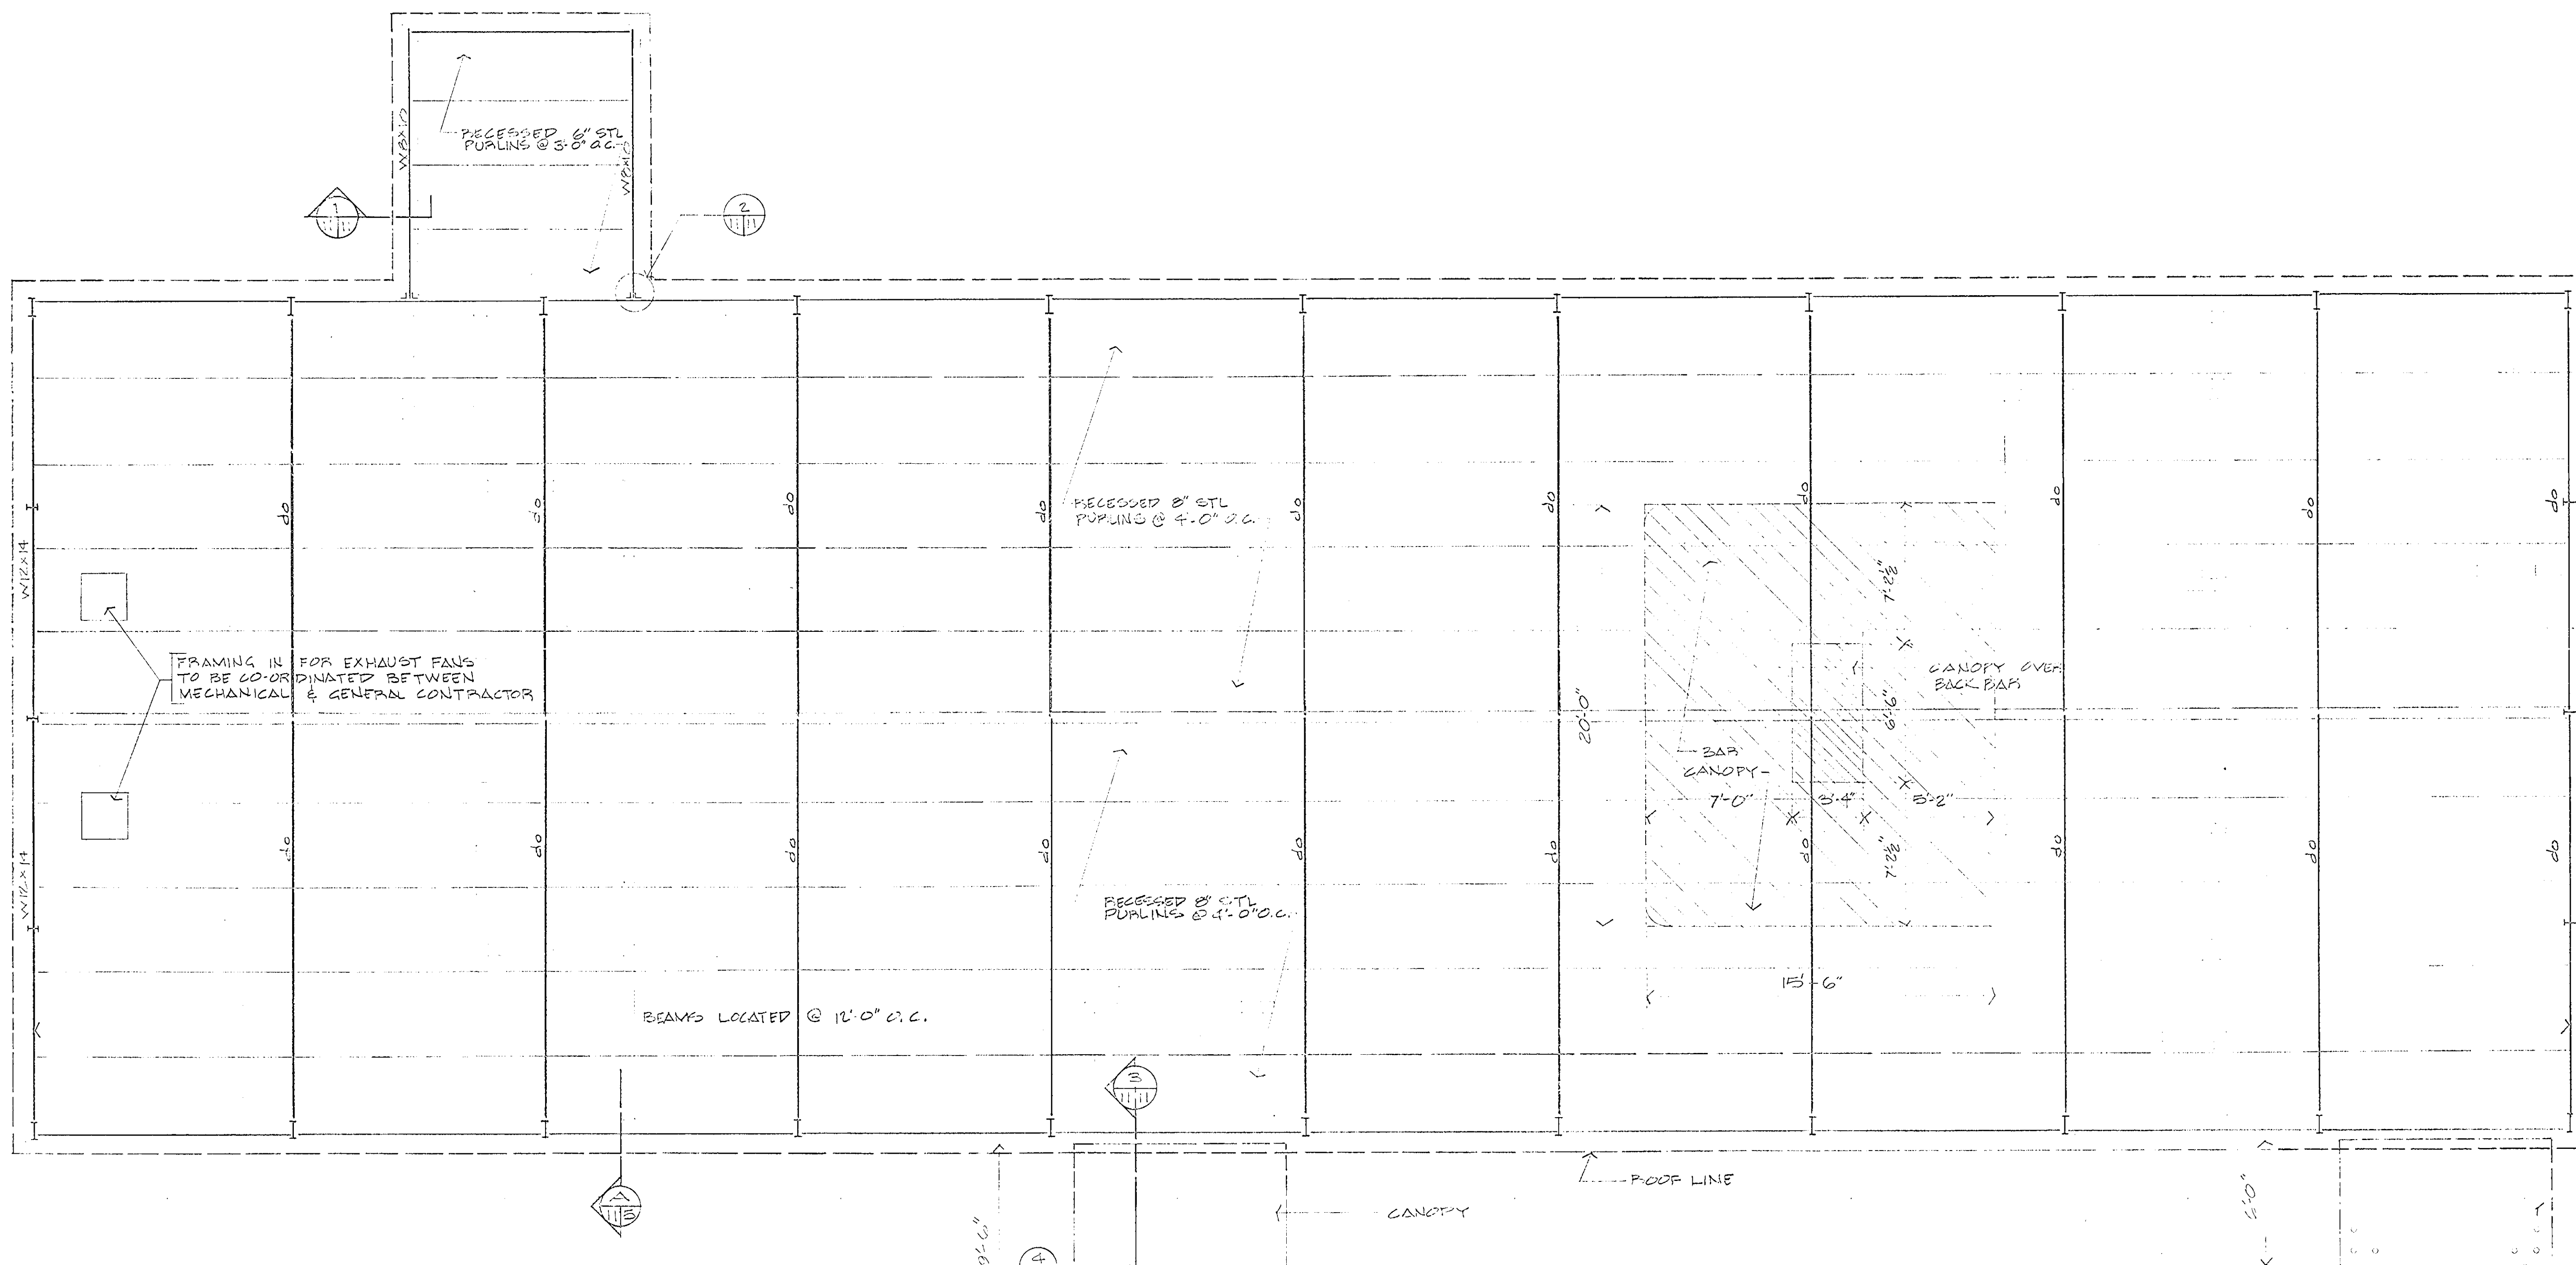

ROOF PLAN
SCALE 1/2"=1'-0"

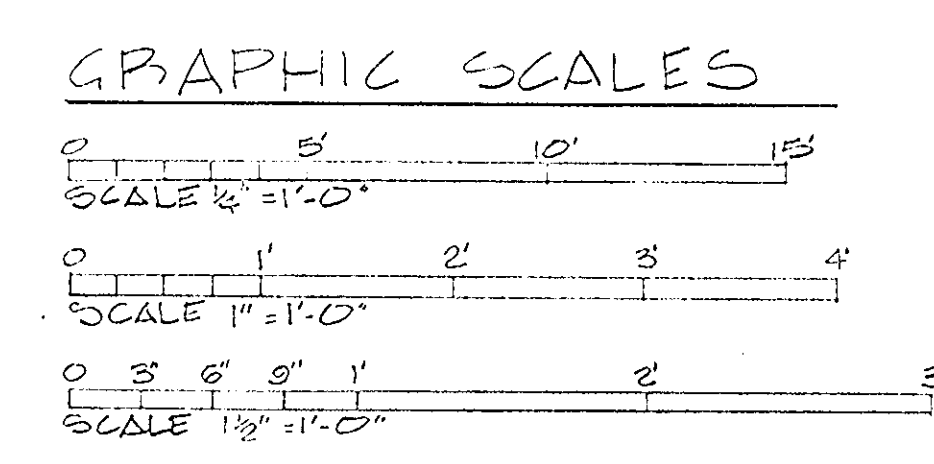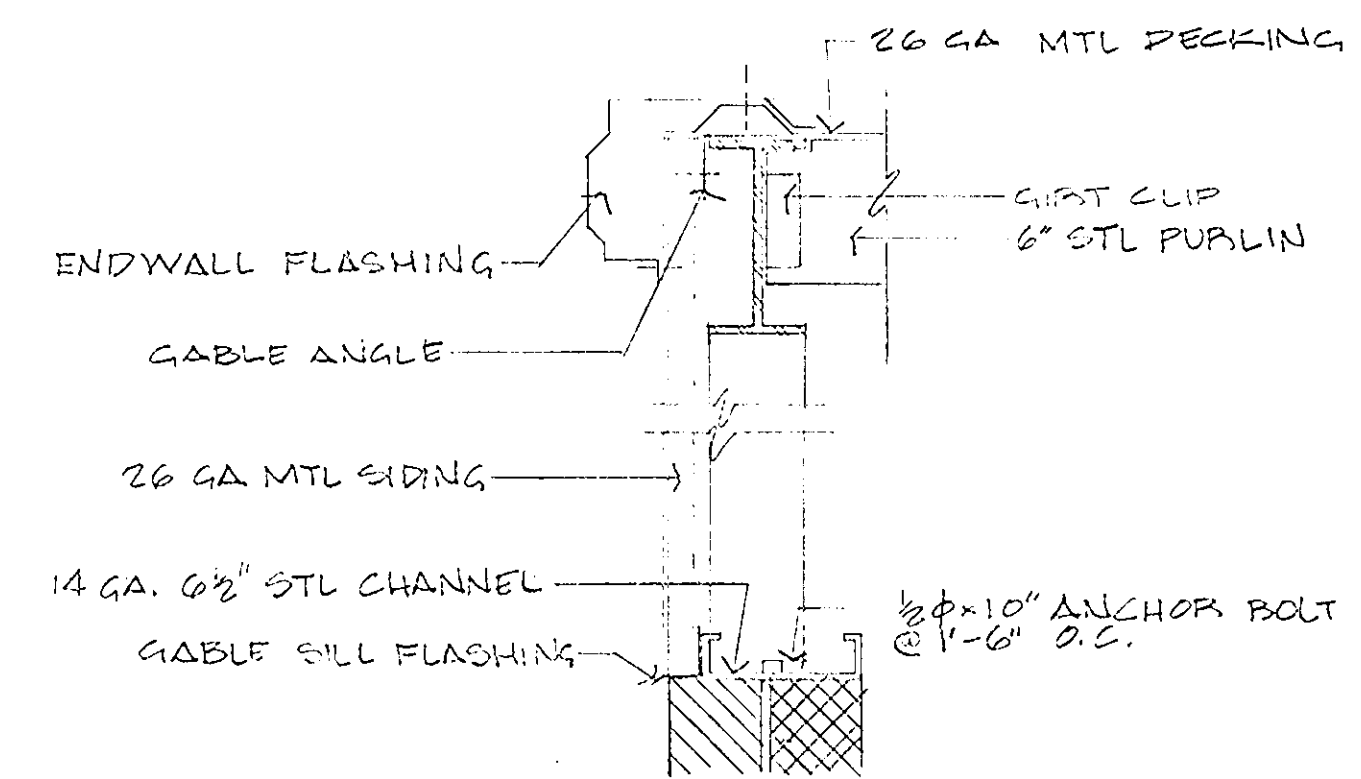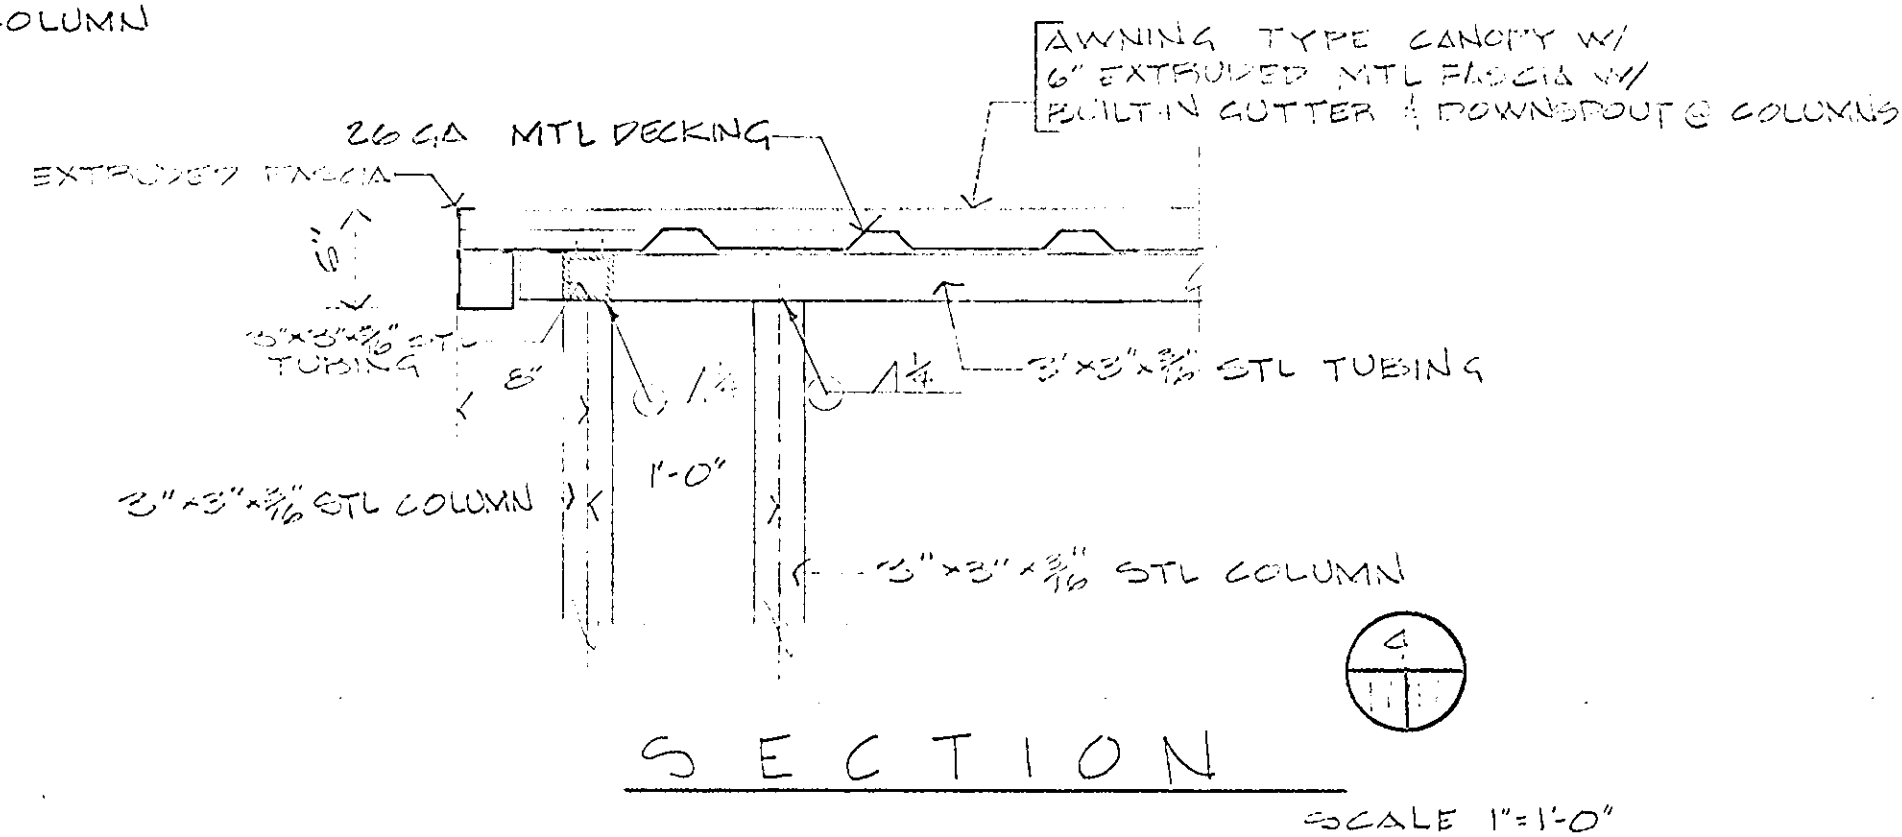


SATISFACTORY TO
26 April 76
DATE [Signature]

PUBLIC WORKS DEPT. MARINE CORPS BASE CAMP LEJEUNE, N.C.		DEPARTMENT OF THE NAVY NAVAL FACILITIES ENGINEERING COMMAND ATLANTIC DIVISION NORFOLK, VIRGINIA	
DESIGNED BY [Signature]	CHECKED BY [Signature]	MARINE CORPS BASE, CAMP LEJEUNE, N.C.	
APPROVED BY [Signature]		NCO CLUB, CAMP GEIGER MARINE CORPS BASE, CAMP LEJEUNE, N.C.	
PUBLIC WORKS OFFICER		ROOF PLAN & DETAILS	
Satisfactory to [Signature]		SIZE F	CODE IDENT NO 80091
COMMANDING GENERAL		NAVFAC DRAWING NO 4011894	
APPROVED BY [Signature]		CONSTR CONTR NO N62470-75-B-0919	
FOR COMMANDER, NAVFAC		SCALE GRAPHIC	SPEC Q5-75-0919
		SHEET 11 OF 18	
		LANTDIV DWG NO	

LEGEND

—RL— REFRIGERANT LIQUID LINE
 —RS— REFRIGERANT Suction LINE
 —G— LP GAS LINE
 THERMOSTAT
 —D— DRAIN LINE

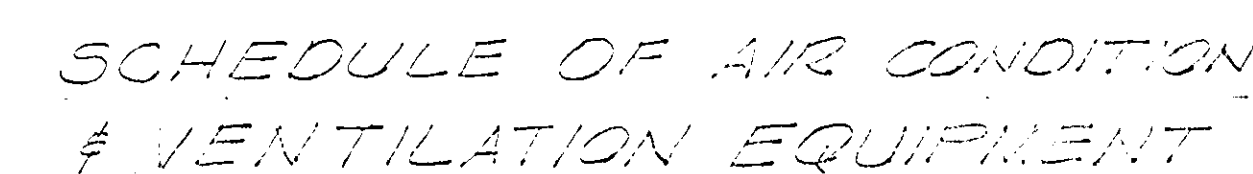

EF-1. 200F INTO, DIRECT ORINE CENTRIFUGAL EXHAUST FAN, ALL ALUMINUM CONSTRUCTION, 450 H.P., 250 CFM @ 1/2" S.F. GRAVITY SHUTTER, UNIT OPERATED BY THERMOSTAT WITH A FIRESTAT IN THE EXHAUST STREAM & A DISCONNECT SWITCH AT THE UNIT.

EF-2 JUMPING INTO ORIENT COAST GUARD CENTRIFUGAL
SWIMMING TANK. ALL WINDS ALIGNED EAST-
SOUTHEAST. HOUR 1000 GPM 4.5 PSI
UNIT OPERATED FROM HEAD
LIGHT SWITCH LOCATED IN BURN
RIGHT WITH EXISTAT LOCATED IN
BURNING. 1000 GPM 4.5 PSI
AT 500 GPM 1000 GPM 4.5 PSI
VENT PIPE 3" WEATHER CAP.


 ATTIC EXHAUST FAN - WALL MOUNTED,
 DIRECT DRIVE PROPELLER FAN
 1/2 HP 208 V. 1 PH. 60 HZ. WITH
 THERMOSTAT CONTROLLED FINGER LOUVER
 FAN EQUIPPED WITH SAFETY GUARD
 ON MOTOR SIDE & DISCONNECT SWITCH
 BREAKSTAY AT UNIT. FAN CONTROLLED
 FROM THERMOSTAT LOCATED IN ATTIC.

AIR HANDLING UNIT DIRECT EXPANSION
WITH CAPACITY OF 15,000 STU/H.
3,000 STU/H WITH REFRIGERANT
TEMPERATURE OF 45°F, SAT 82°F DB,
74% WS, LAT 68.4°N 06. 41.1°E WS.
FAN MOTOR APPROX SHP TO SUPPLY
GOOD FLOW OF AIR EXTERNAL S.P. UNIT
SHALL HAVE DOWN STAIR HEATER TO
GIVE TEMPERING FLOWING AIR.
HEATING CAPACITY OF 15,000 STU/H.
WITH CAT @ 30°F.

BR4 ATT'D INTO CRIBST ONE CENTRIFUGAL
EXHAUST FAN ALL ALUMINUM CONST-
RUCTION 150 HP, 155 GPM @ 15' LIFT.
UNIT OPERATED FROM SWITCH ON
LIGHTS. LIGHTS IN CRIBAGE
CRIB- UNIT BRUNNED W/ RICEBUT
3 ON CONNECT, 15" THRU SCOF
W/ VENT PIPE & WEATHER CAP

EPS WALL INTO OBJECT ORIVE CENTRIFUGAL
EXHAUST FAN, ALL ALUMINUM CON-
STRUCTION 110 HP, 550 CFM @ 1/2" SP.
WITH GRAVITY LOUVER - UNIT OPERATED
FROM WALL SWITCH WITH PILOT LIGHT.

EF-6 ROOF INTO DIRECT DRIVE EXHAUST
FAN 50 CFM @ 1/8" S.P. UNIT OPER-
ATED FROM LIGHT SWITCH IN HEAD.
VENT THRU ROOF WITH 6" DIA. $\frac{1}{2}$ "
WEATHER CAP.

KITCHEN SUPPLY & EXHAUST AIR HOOD- SHALL
SUPPLY & EXHAUST APPROX 6000 CFM
WITH CONNECTIONS FOR HOT WATER &
GAS TO SERVE HOOD. UNIT SHALL
HAVE AUTOMATIC RISE DAMPER &
DETECTOR SYSTEM.

FLOOR PLAN SCALE: 4" = 1'-0"




SCALE - $\frac{1}{4}" = 1' - 0"$




SCALE - 1" = 1'-0"

PUBLIC WORKS DEPT. MARINE CORPS BASE CAMP LEJEUNE, N.C.			DEPARTMENT OF THE NAVY NAVAL FACILITIES ENGINEERING COMMAND ATLANTIC DIVISION		
DES. <i>12/1</i> DR. <i>12/1</i> CHK. <i>12/1</i> PROJ MGR <i>12/1</i> C. <i>12/1</i> E. <i>12/1</i> APPROVED <i>12/1</i> DATE <i>12/1</i> PUBLIC WORKS OFFICER SATISFACTORY TO DATE			NAVAL STATION NORFOLK, VIRGINIA MARINE CORPS BASE, CAMP LEJEUNE, N.C. NCO CLUB, CAMP GEIGER MARINE CORPS BASE, CAMP LEJEUNE, N.C. HEATING & AIR CONDITIONING PLAN		
COMMANDING GENERAL EPD RVD HD APPROVED <i>12/1</i> DATE <i>12/1</i>			SIZE CODE IDENT NO F 80091 NAVFAC DRAWING NO 4011895 CONSTR CONTR NO N62470-75-B-0915		
SCALE GRAPHIC SPEC			05-75-0919		SHEET 12 OF 18


REVISIONS			
SYM	DESCRIPTION	DATE	APPROVED

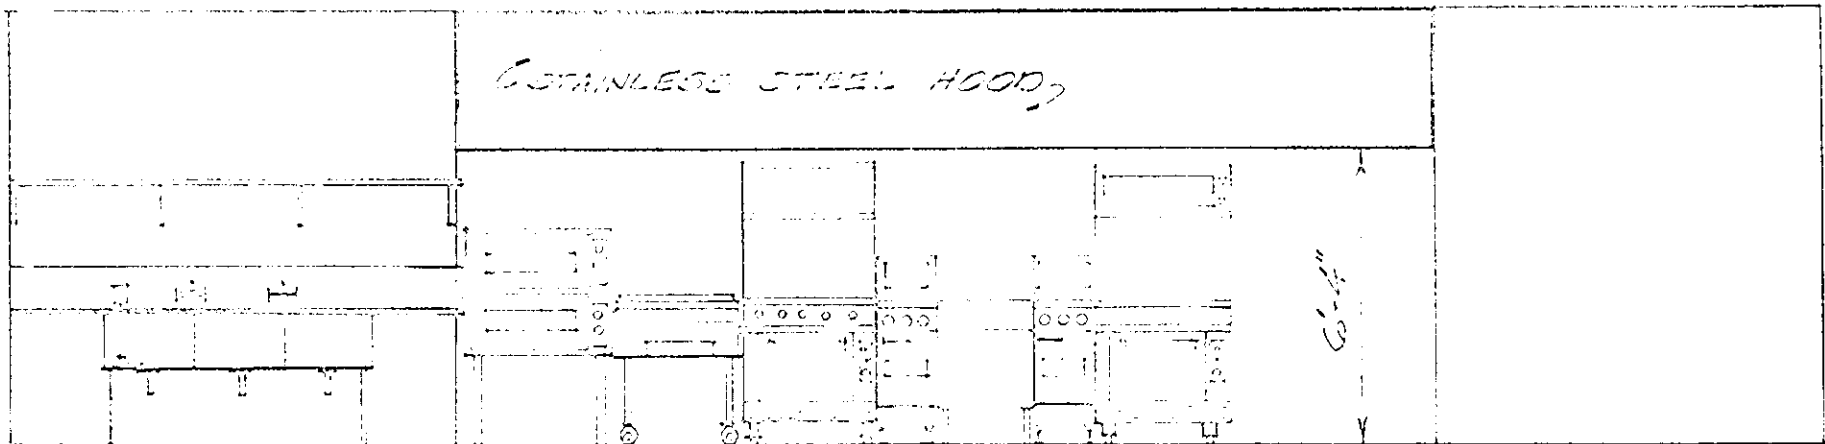


ELEVATION 2 SCALE 1/4" = 1'-0"

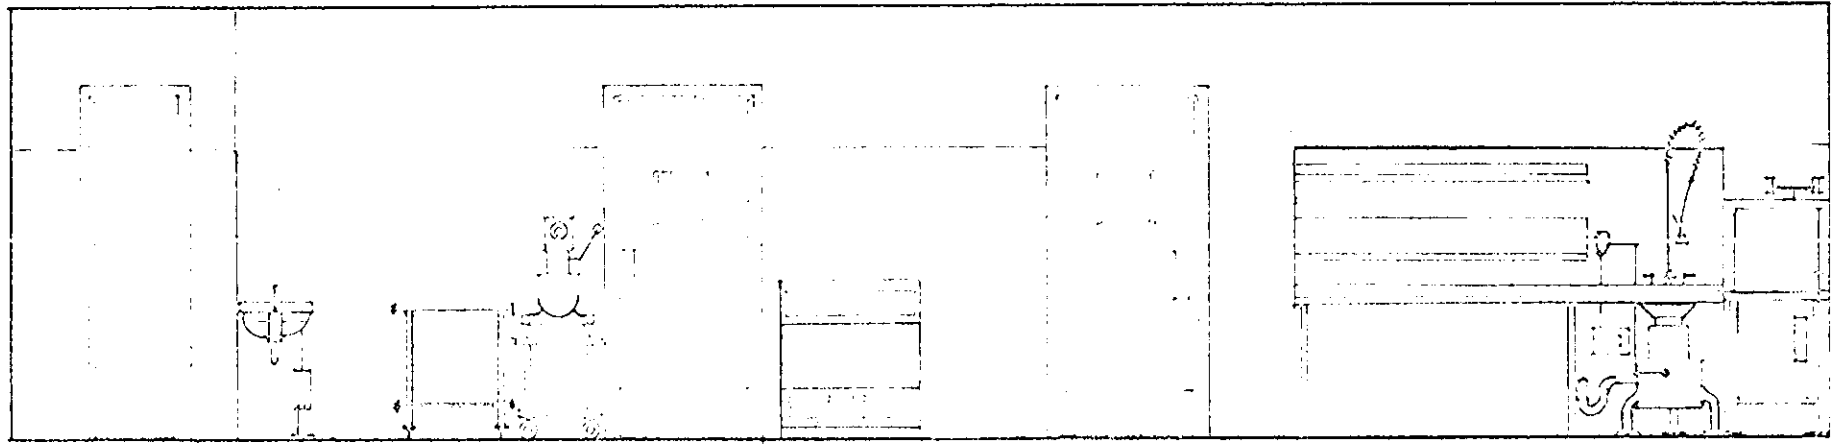


ELEVATION 2 SCALE 1/4" = 1'-0"

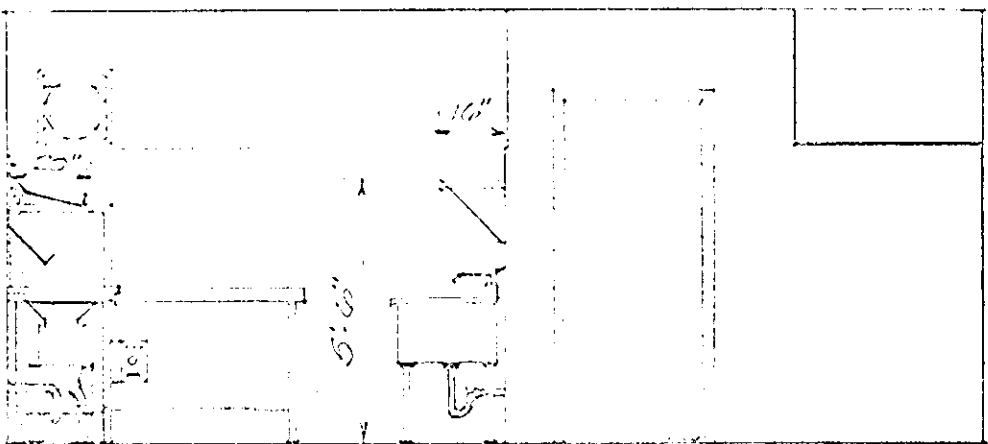

ELEVATION 1 SCALE 1/4" = 1'-0"

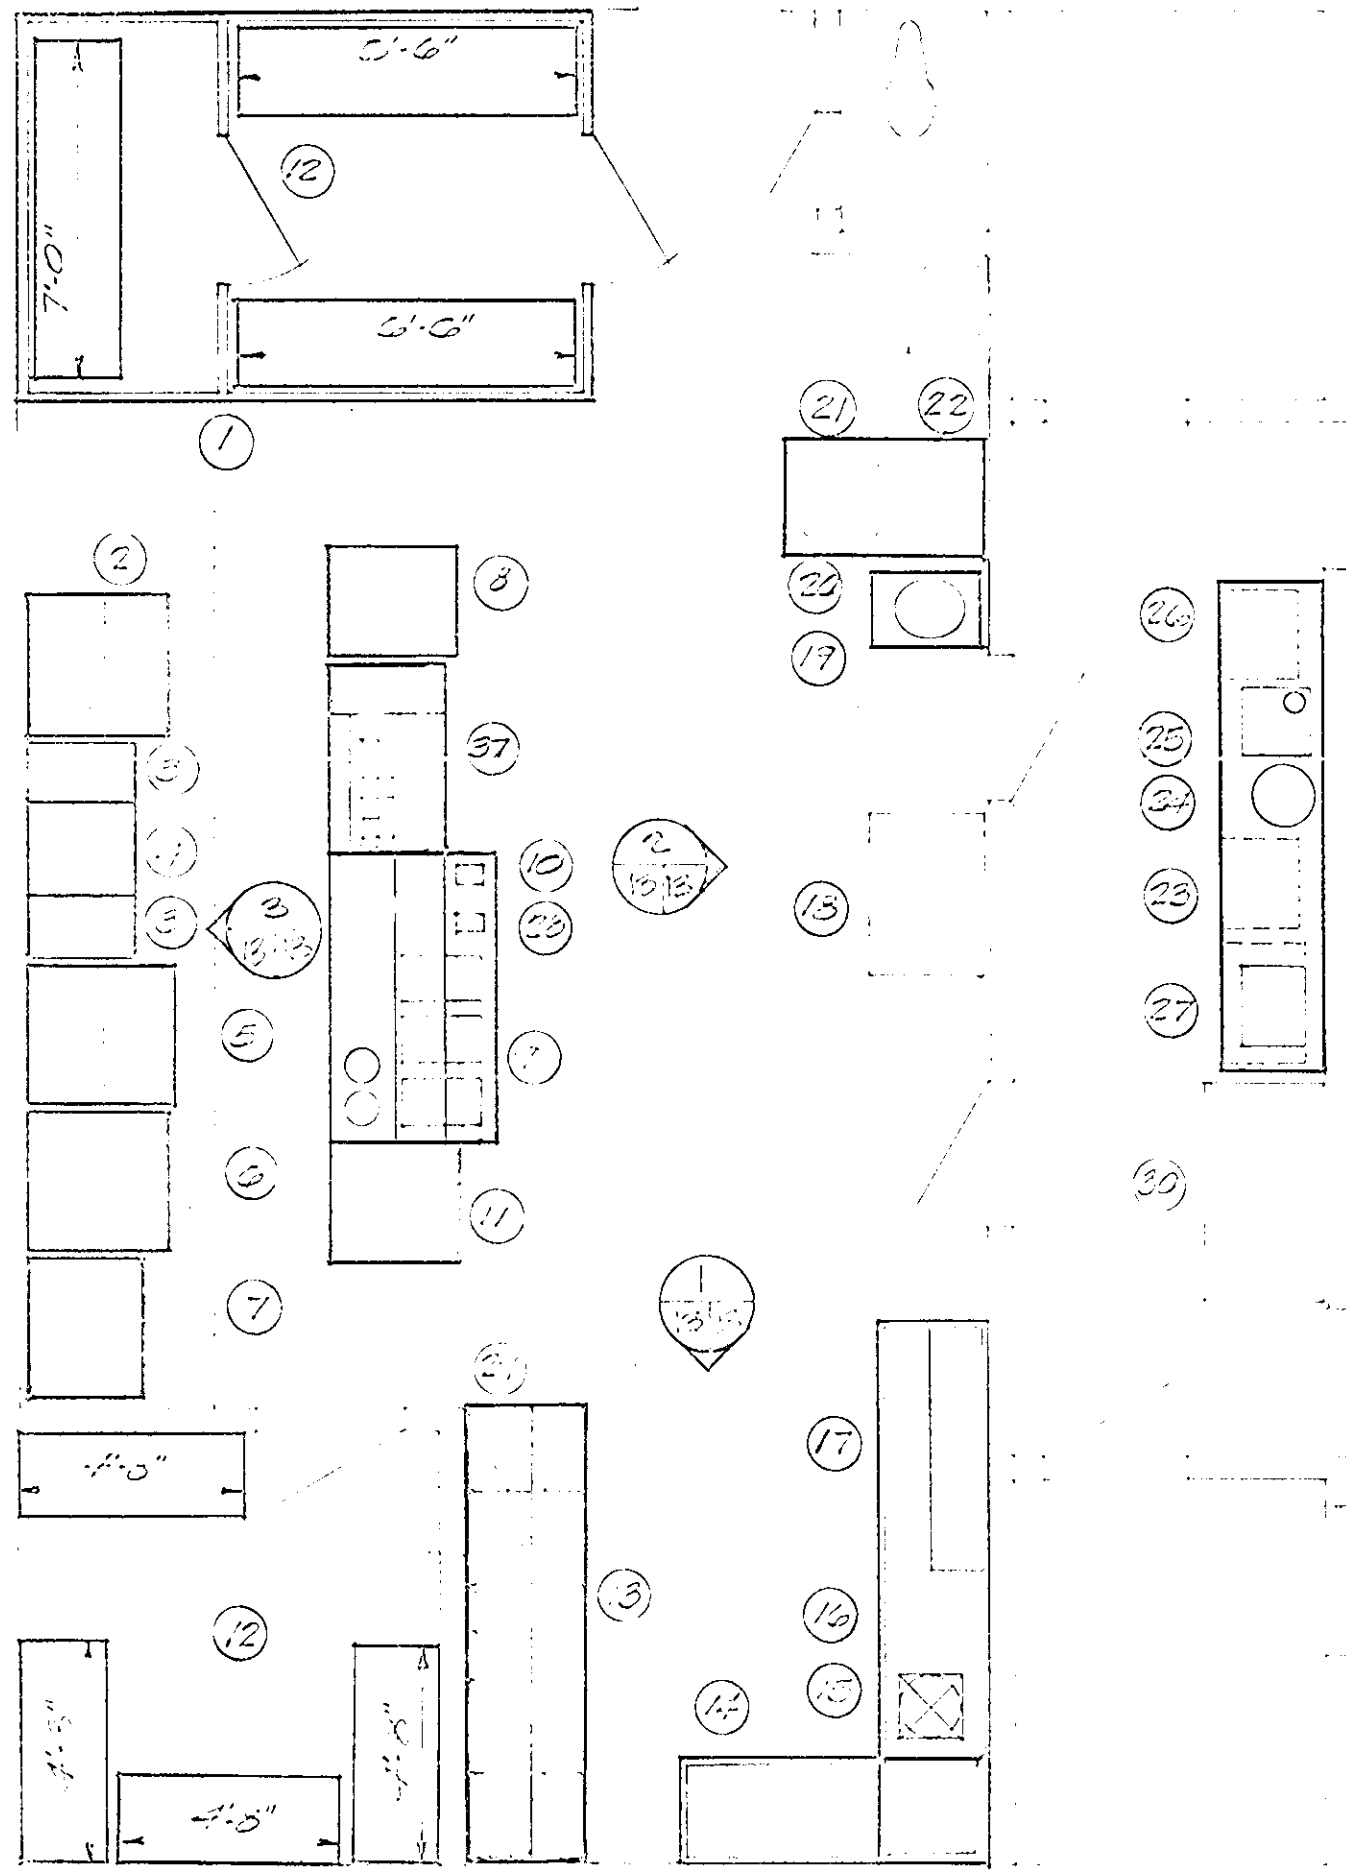

PLAN - KITCHEN & BAR EQUIPMENT SCALE 1/4" = 1'-0"

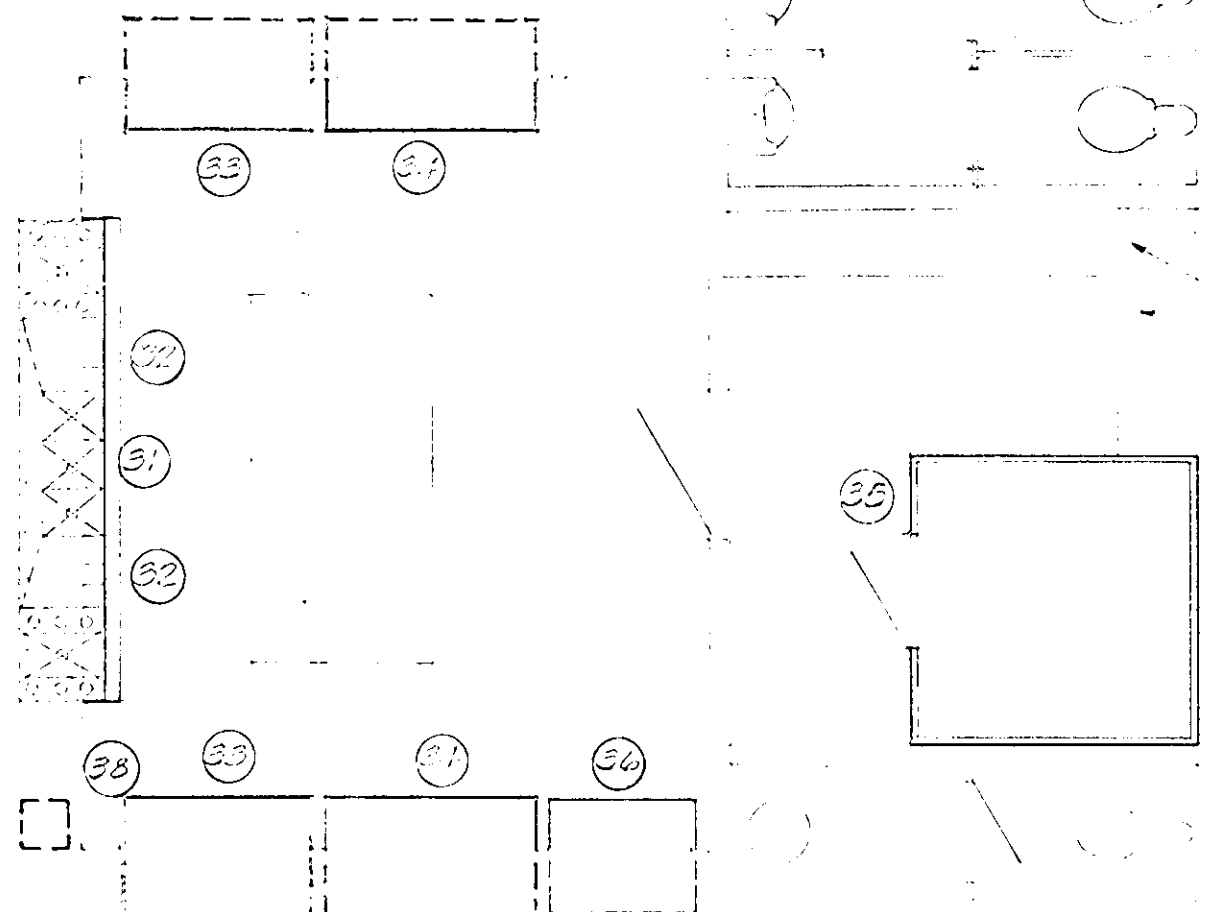


SEE ARCHITECTURAL SHEET FOR SHELVING

SCHEDULE KITCHEN & BAR EQUIPMENT

NR	ITEM	ELECTRICAL PLUMBING V ST PH AMP KW HP DEN CM HM GAS	REMARKS
1	WALK-IN REFRIGERATOR	208 60 3 17.3	184, 208V, 14 CIRCOST REQUIRED
2	HOT TOP RANGE WITH OVEN & SALAMANDER	208 60 3 57.7	
3	DEEP FAT Fryer	208 60 3 17.3	2 EA ON CASTERS
4	JUMP STAND		
5	GRIDDLE	208 60 3 16.2	WITH OPEN STORAGE & CASTERS
6	CHAR-BROILER		25000 BTU - WITH CASTERS
7	PIZZA OVEN	208 60 3 9.6	GOVERNMENT FURNISHED
8	REACH-IN REFRIGERATOR	120 60 1 4	ON CASTERS
9	CHEF TABLE	208 60 1 3.4	15' 6" 6" PLUS WATER REC. FUTURE
10	TOASTER	208 60 1 2.7	
11	REACH-IN FREEZER	120 60 1 6	ON CASTERS
12	SHELVING		ALL 180" 20" WIDE PLAN
13	SCULLERY SINK	208 60 3 4.5	15' 6" 6" 3" FSC LENSING - WITH CASTERS
14	CLEAN DICH TABLE		THREE COMPARTMENT SINK W/ ELECTRIC HEATING ELEMENT
15	DISHWASHER	208 60 3 20	1 2" 1 1/2" WITH ELECTRIC BOOSTER HEATER
16	DIST. COOLER	208 60 3 4.4	5 2" 3" 1/2" WITH POSITIVE PLUCH FEATURE
17	POUR-ONSE TABLE		
18	ICE MACHINE	120 60 1 6	15' 6" 6" GOVT FURNISHED, CONTRACTOR TO RUN & STUE UTILITIES @ UNIT
19	MIXER	120 60 1 6	20 QUART CAPACITY
20	PORTABLE MIXER STAND		WITH CASTERS
21	WEEK TABLE		
22	SLIDER	120 60 1 4	

NR	ITEM	ELECTRICAL PLUMBING V ST PH AMP KW HP DEN CM HM GAS	REMARKS
23	WATER DISPENSER	120 60 1 30	15' 6" INCORPORATED INTO NR 25
24	ICE TEA URN		
25	MINI-MART STATION		2 EA SET END TO END
26	ROLL WARMER	120 60 1 7	INCORPORATED INTO NR 25
27	COFFEE MAKER	120 60 1 27	3" SPECIAL ELECTRIC PLUG
28	TOASTER	208 60 1 1.8	
29	CLEAN POT & PAN SHELF		
30	DEEPT REFRIGERATOR	120 60 1 6	GOVT FURNISHED, CONTRACTOR TO RUN & STUE UTILITIES @ UNIT
31	UNDER BAR SINK		15' 6" 6"
32	FLEXIBLE BAR FOUNTAIN	120 60 1 3	GOVT FURNISHED, CONTRACTOR TO RUN & STUE UTILITIES @ UNIT
33	DRAFT BEER BOX	120 60 1 6	1" 2 EA.
34	BEVERAGE COOLER	120 60 1 4	1" 2 EA.
35	WALK-IN COOLER	208 60 1 6	
36	ICE MACHINE	120 60 1 6	1 1/2" 15' 6" 6" GOVT FURNISHED, CONTRACTOR TO RUN & STUE UTILITIES @ UNIT
37	SANDWICH UNIT	120 60 1 5	3" GOVT FURNISHED, CONTRACTOR TO RUN & STUE UTILITIES @ UNIT
38	SHRIMP TRAYS & ASIA-MATHS UNIT	120 60 1 5	1 1/2" GOVT FURNISHED, CONTRACTOR TO RUN & STUE UTILITIES @ UNIT

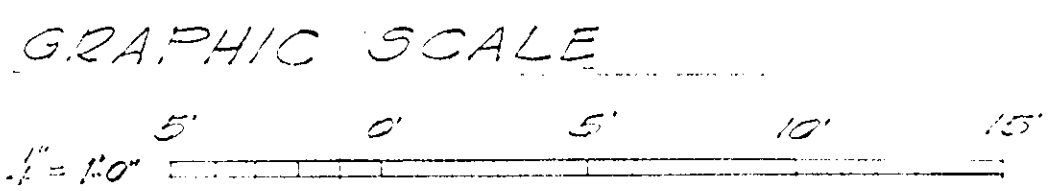


SATISFACTORY TO


DATE 26 Dec 76

PUBLIC WORKS DEPT. MARINE CORPS BASE CAMP LEJEUNE, N.C.		DEPARTMENT OF THE NAVY NAVAL FACILITIES ENGINEERING COMMAND ATLANTIC DIVISION MARINE CORPS BASE, CAMP LEJEUNE, N.C.	
DES. 201 OR 202	CHK. 201	NCO CLUB, CAMP GEIGER MARINE CORPS BASE, CAMP LEJEUNE, N.C. KITCHEN & BAR SCHEDULE W/ INTERIOR ELEVATIONS	
PROJ MGR. 2001 OR 202	DATE 26 Dec 76	SIZE F	CODE IDENT NO 80091
APPROVED. 201 OR 202	DATE 26 Dec 76	NAVFAC DRAWING NO 4011896	
PUBLIC WORKS OFFICER		CONSTR CONTR NO N62470-75-B-0919	
SATISFACTORY TO		SCALE GRAPHIC SPEC 05-75-0919	
COMMANDING GENERAL		SHEET 13 OF 18	
EFD RVD		LANTDIV DWG NO	
HD DIR			
APPROVED. 201 OR 202			
DATE 26 Dec 76			
FOR COMMANDER, NAVFAC			


REVISIONS			
SYM	DESCRIPTION	DATE	APPROVED

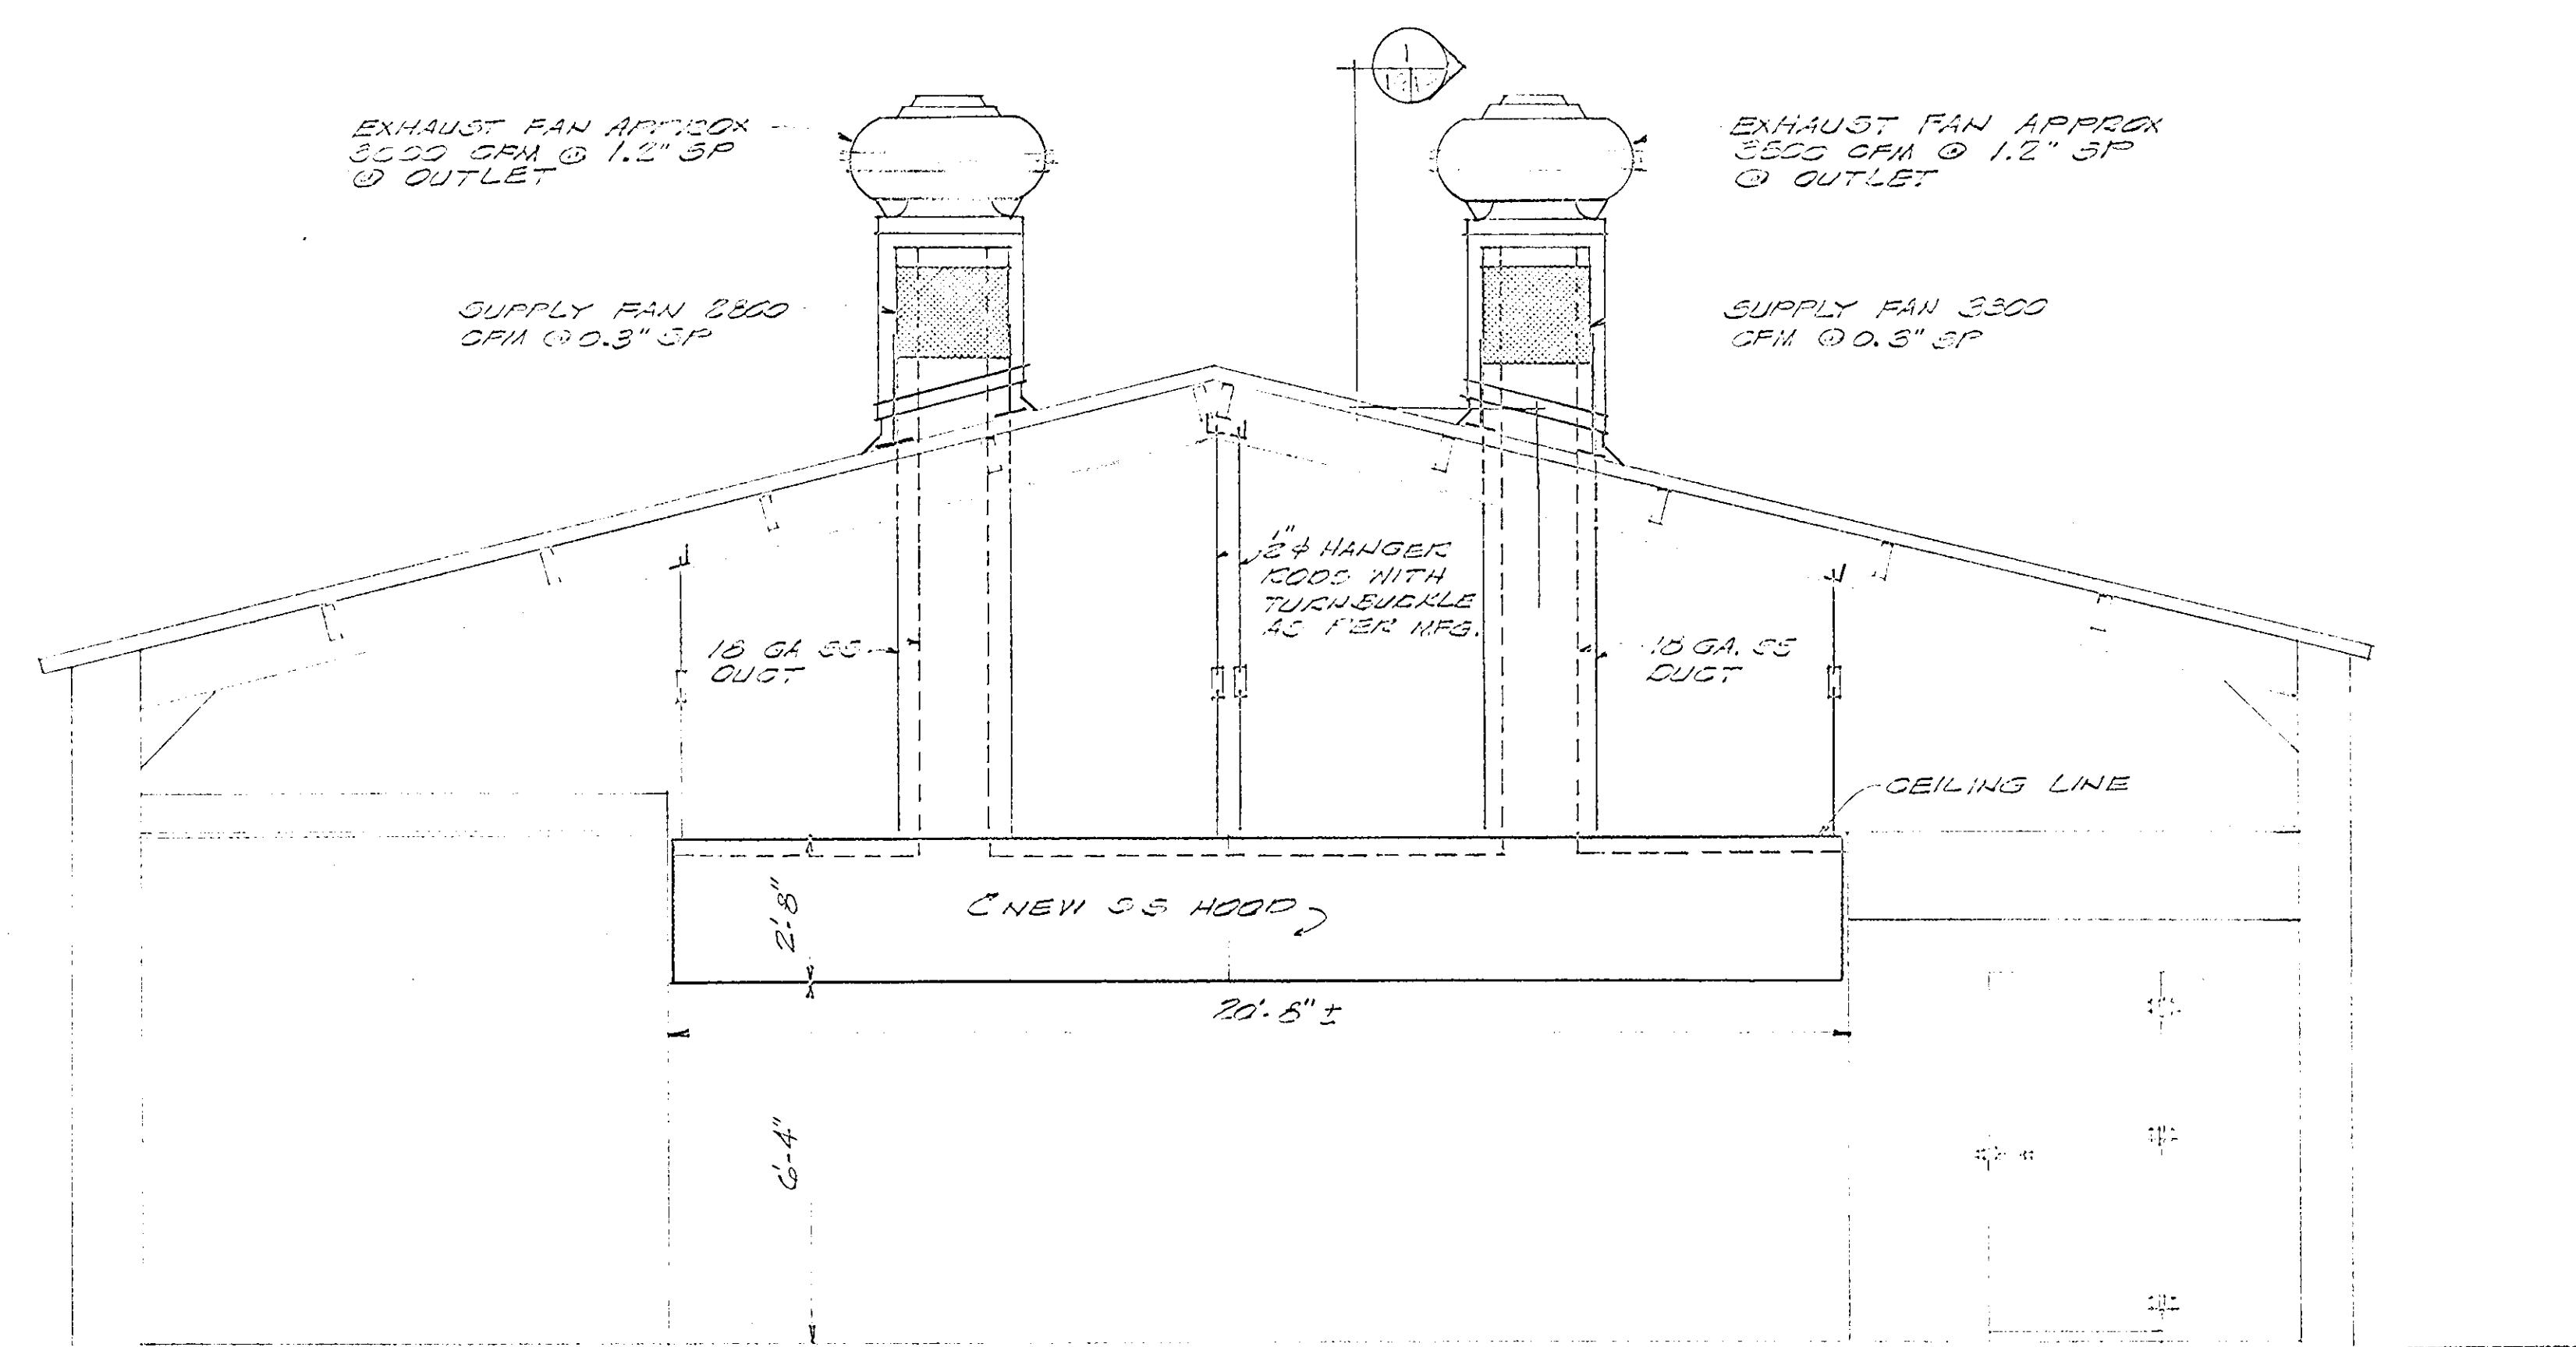


SECTION 0 SCALE - 3/8" = 1'-0"

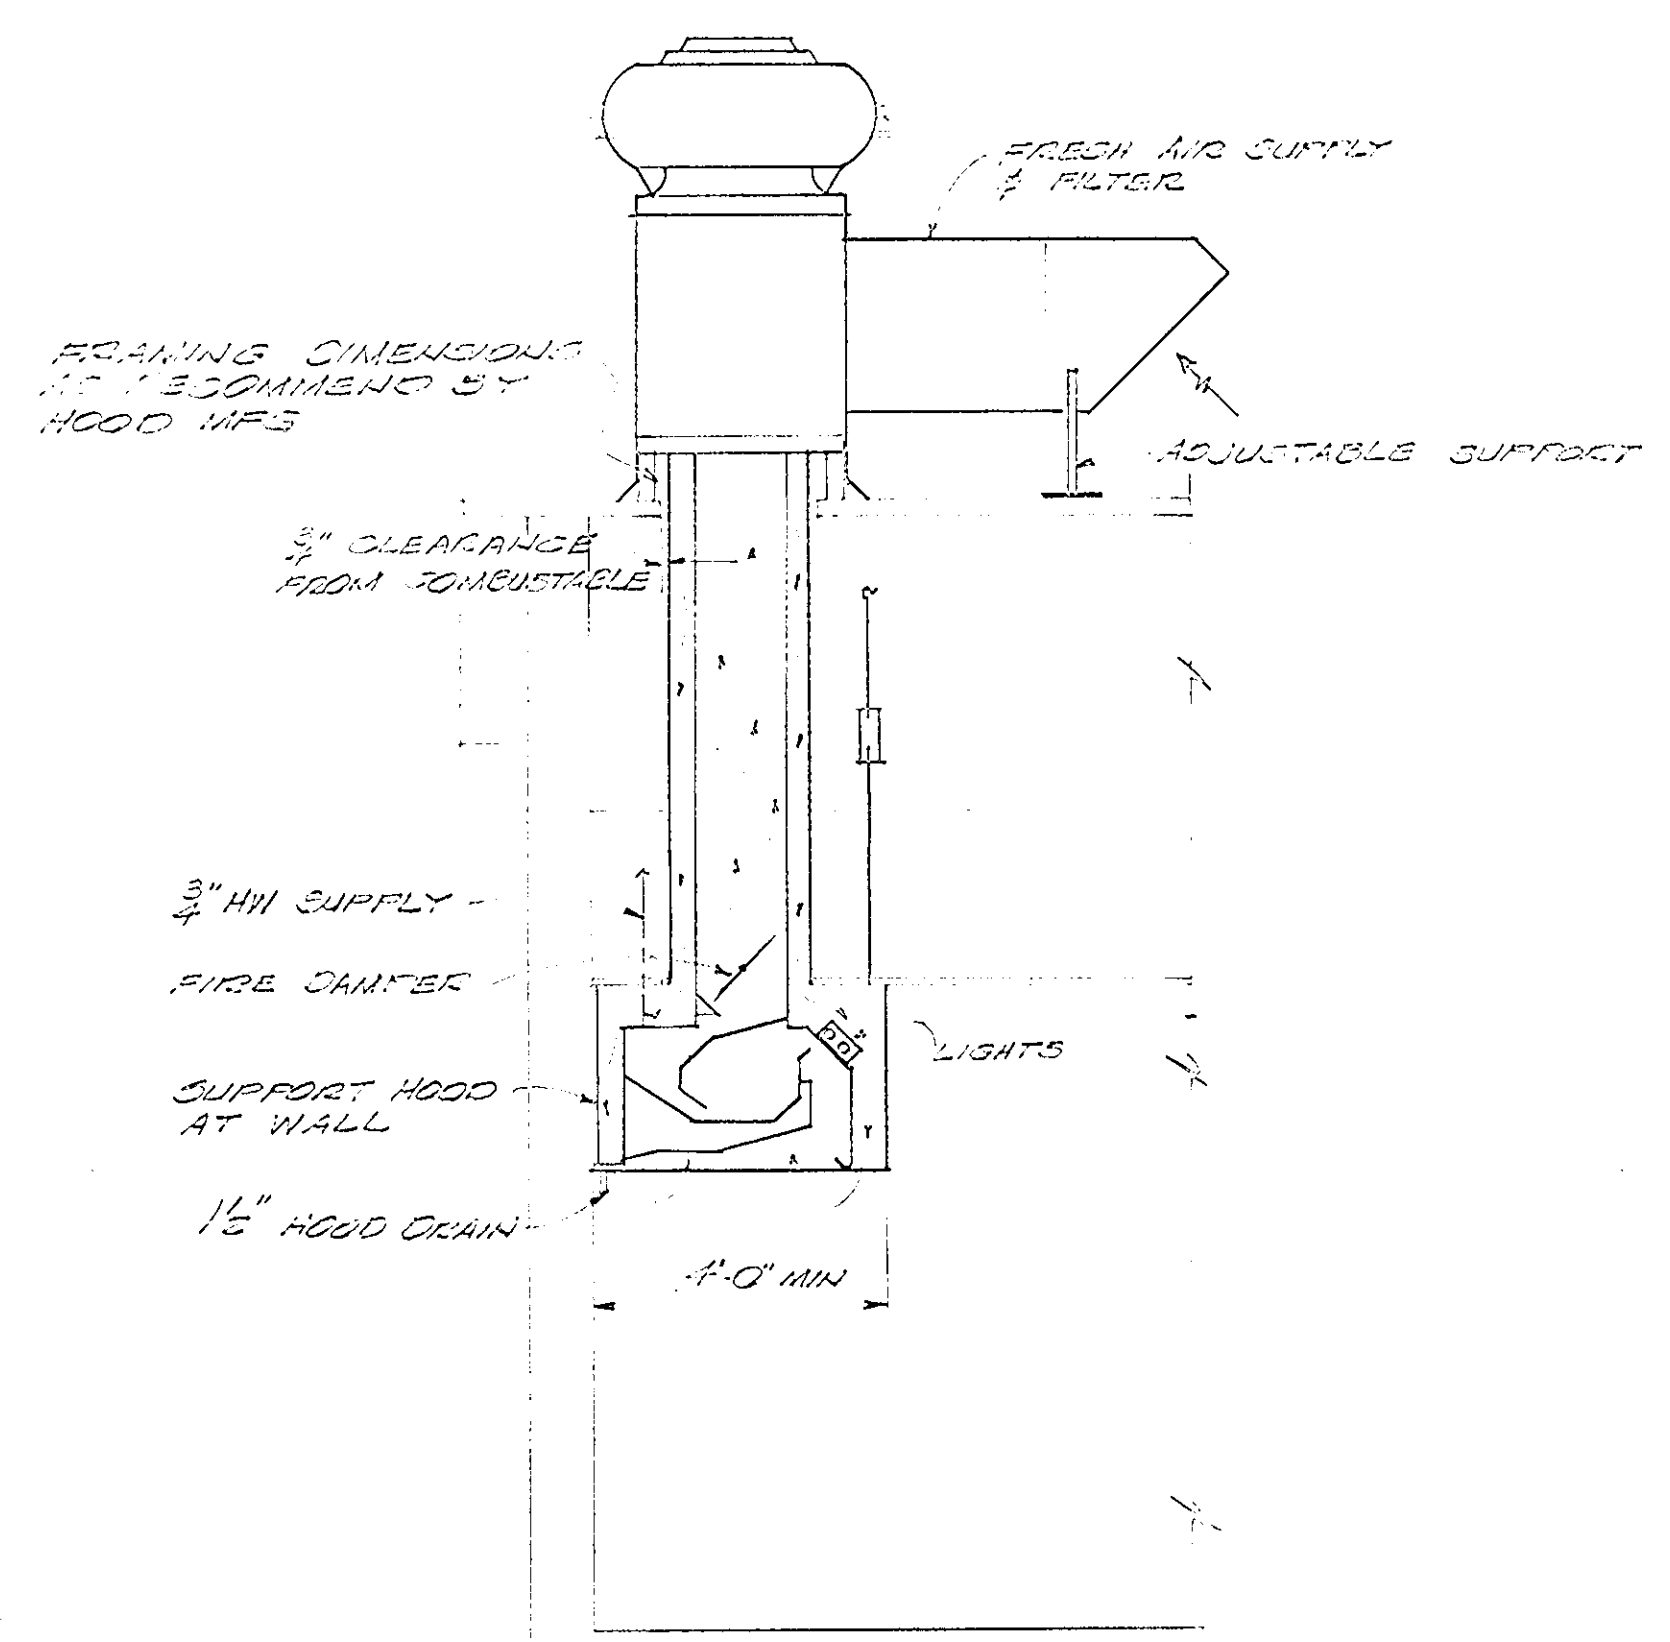


SECTION 1 SCALE - 3/8" = 1'-0"

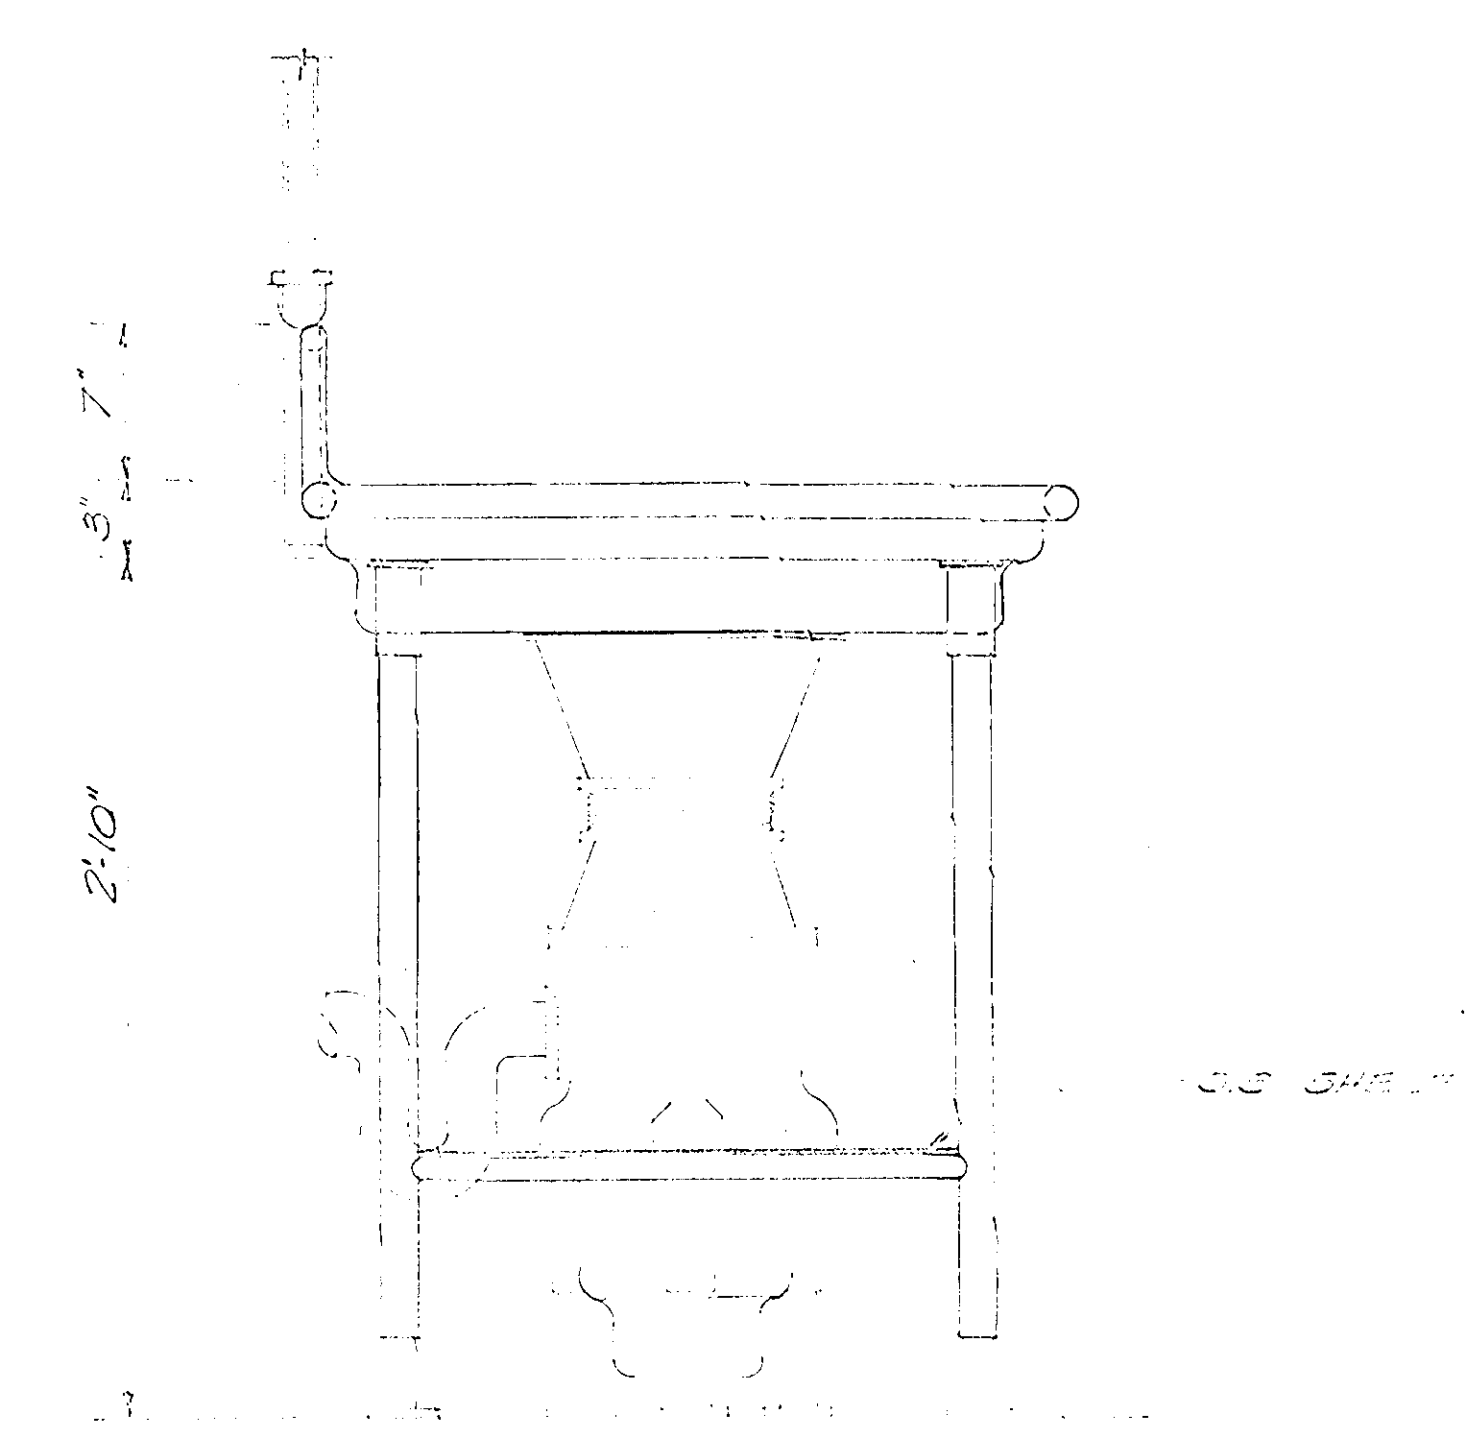


ELEVATION 2 SCALE - 3/8" = 1'-0"

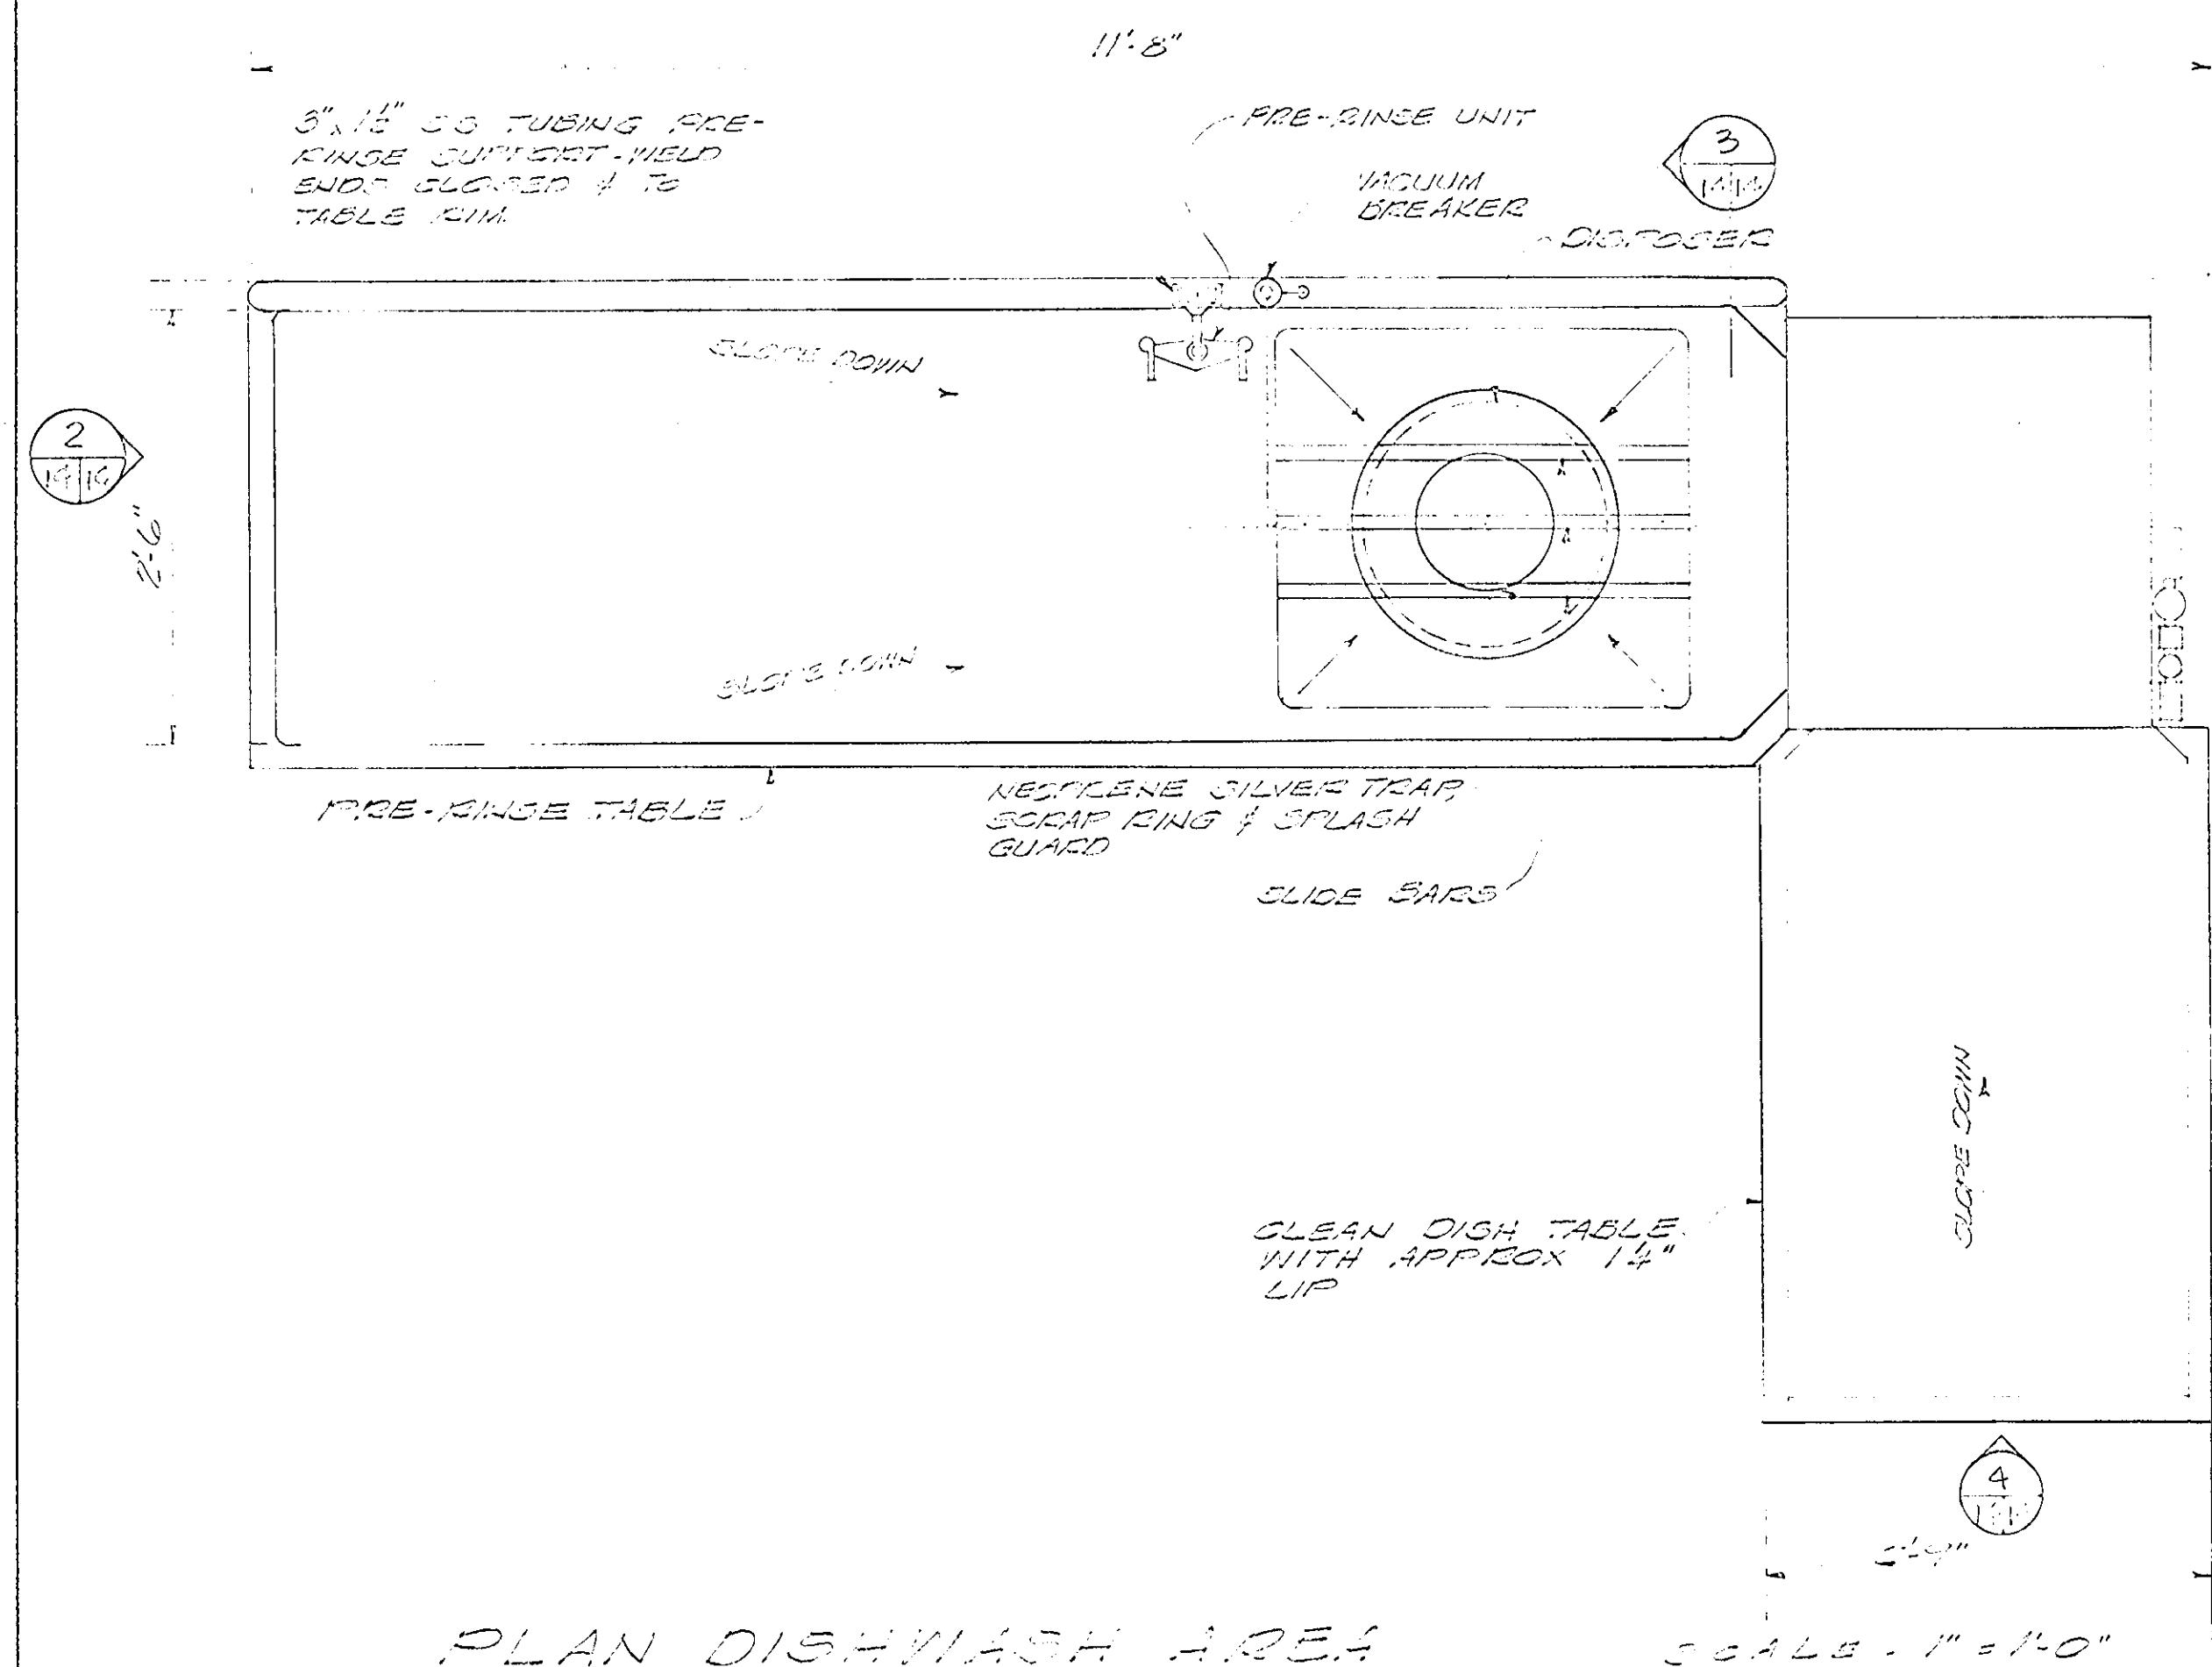


PLAN DISHWASH AREA SCALE - 1/2" = 1'-0"

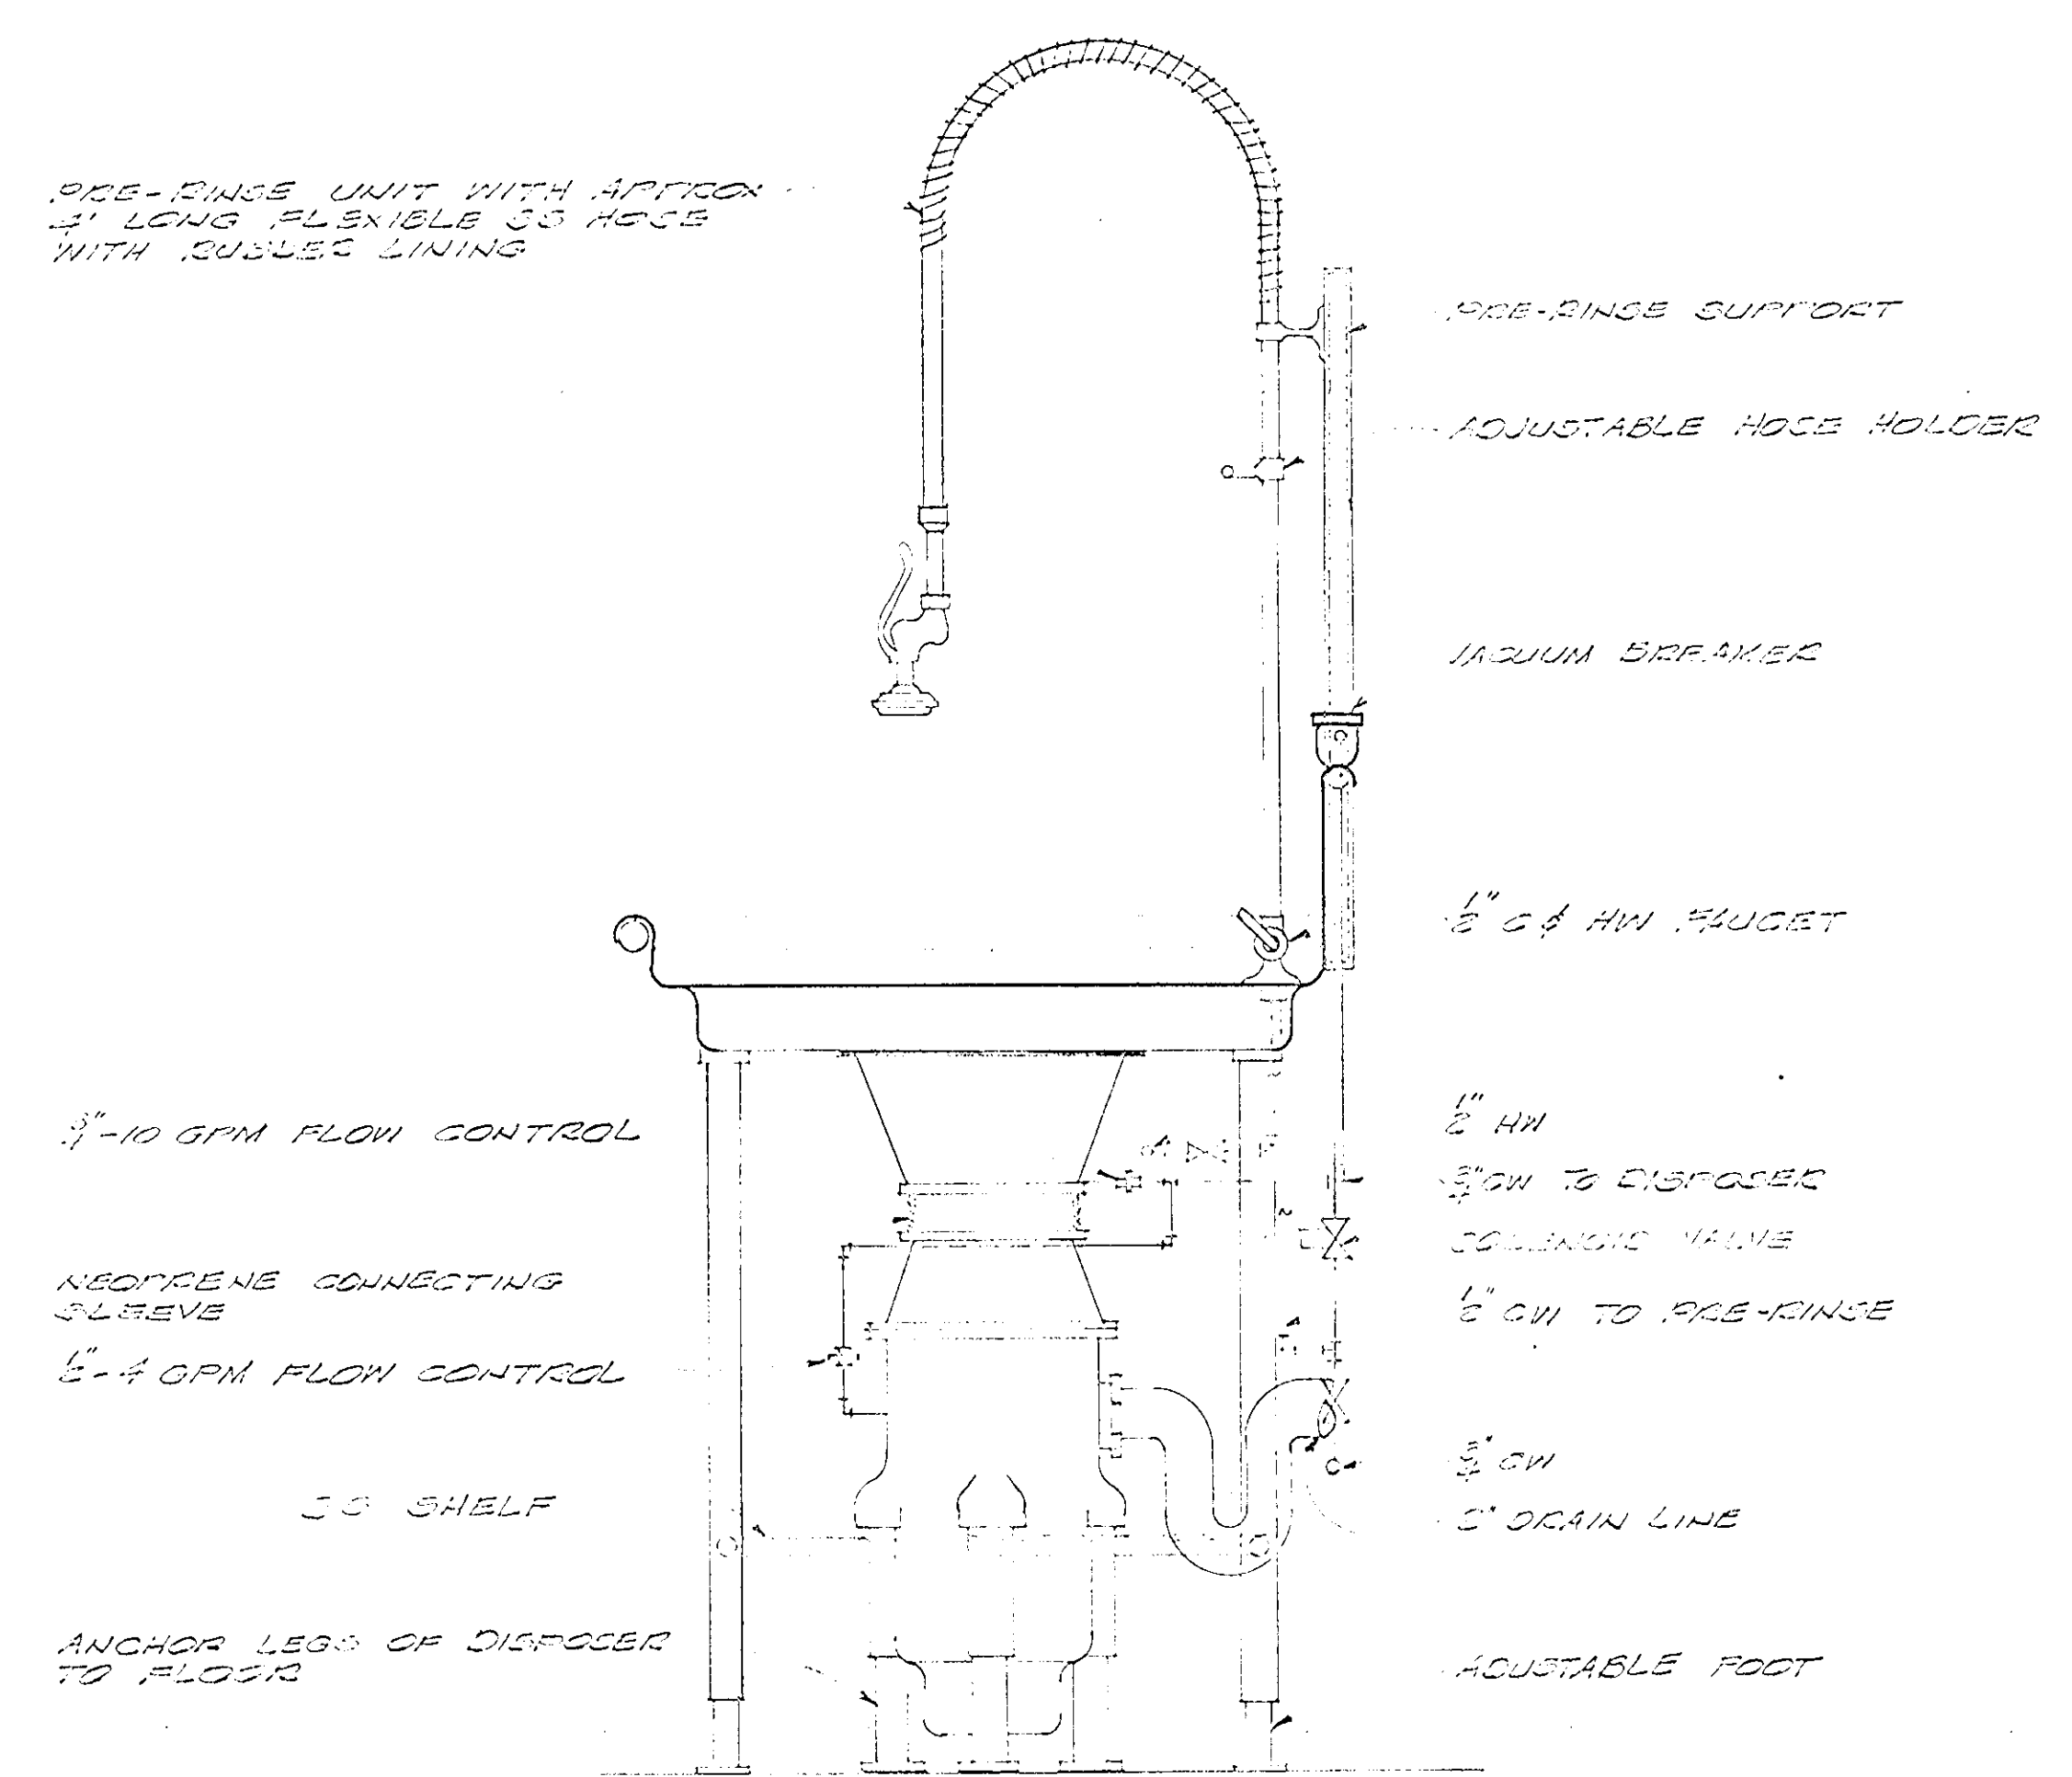

SECTION 3 SCALE - 1/2" = 1'-0"
(TWO SLIDE RACKS SHOWN IN SECTION)

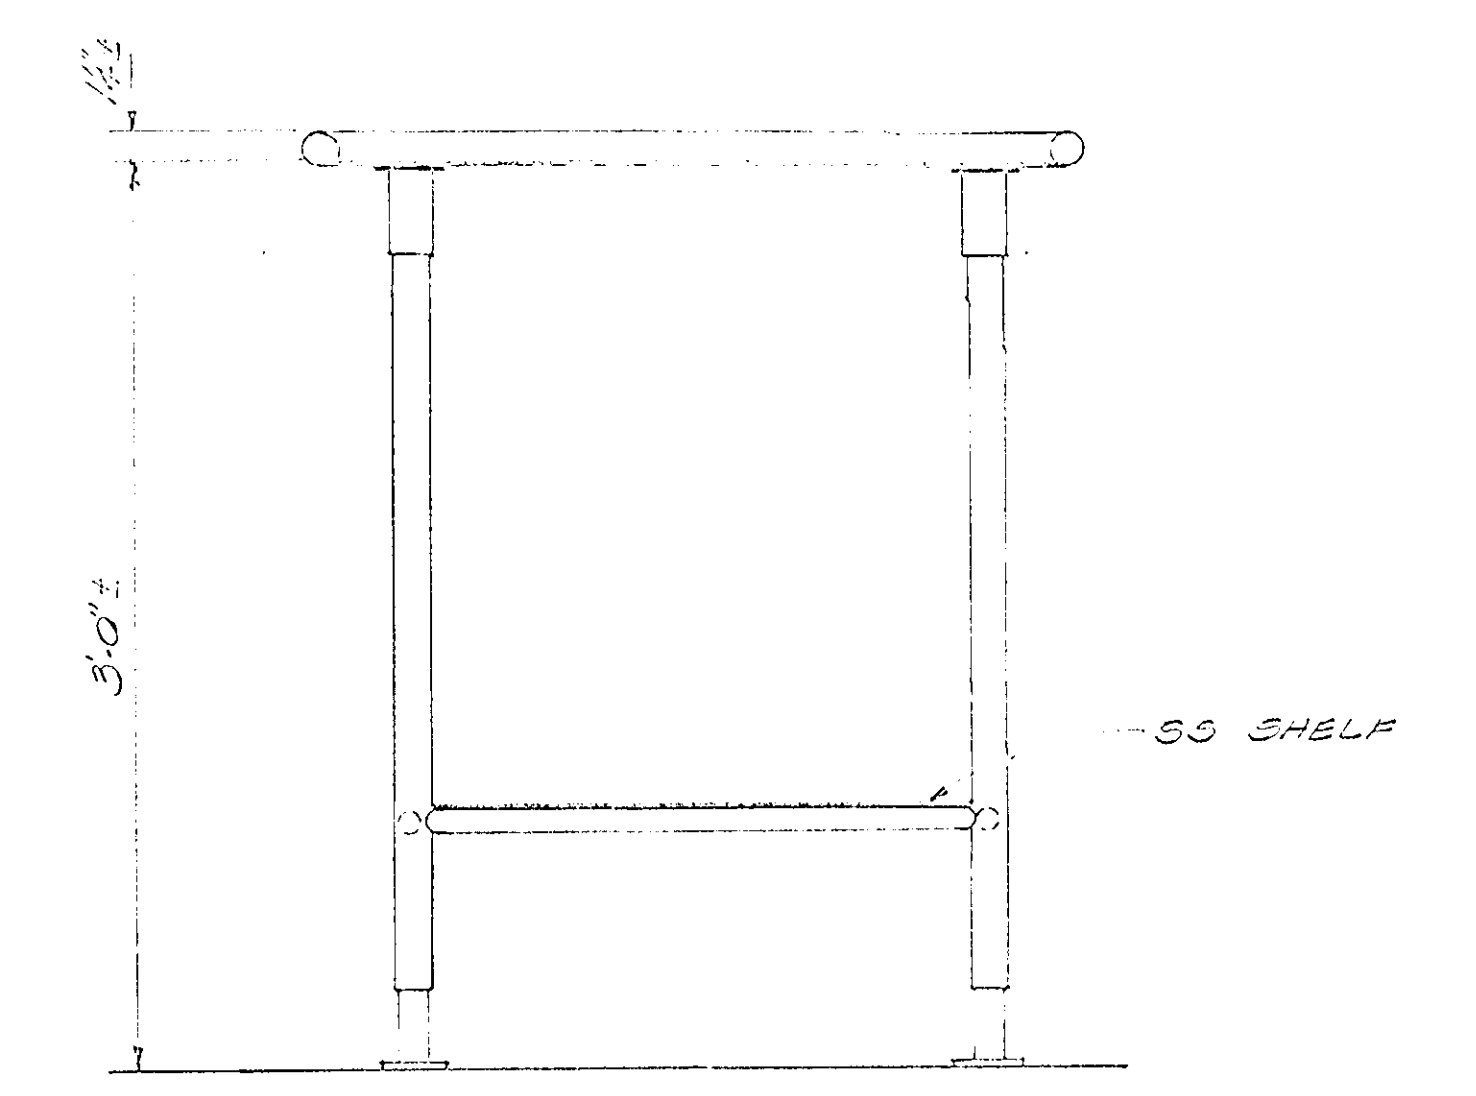

ELEVATION 4 SCALE - 1/2" = 1'-0"

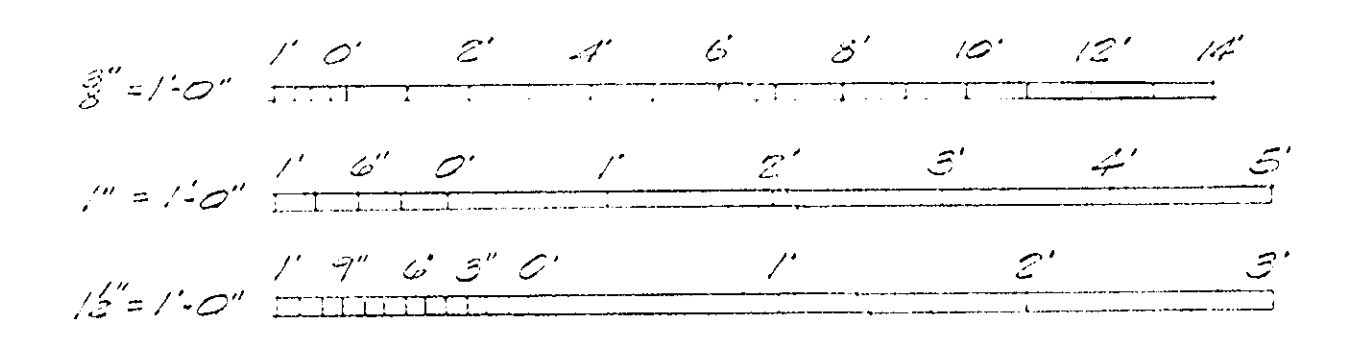


SATISFACTORY TO
DATE 26 Oct 76

PUBLIC WORKS DEPT. MARINE CORPS BASE CAMP LEJEUNE, N.C.		DEPARTMENT OF THE NAVY NAVAL FACILITIES ENGINEERING COMMAND ATLANTIC DIVISION MARINE CORPS BASE, CAMP LEJEUNE, N.C.	
DES/CHK/APP	PROJ MSR	DATE	DATE
APPROVED		DATE	
PUBLIC WORKS OFFICER		DATE	
Satisfactory to		DATE	
COMMANDING GENERAL		DATE	
EFD	RVD	DATE	
ND	DIR	DATE	
APPROVED		DATE	
FOR COMMANDER, NAVFAC		DATE	
SIZE	CODE IDENT NO	NAVFAC DRAWING NO	
F	80091	4011897	
SCALE GRAPHIC		CONSTR CONTR NO N62470-75-B-0919	
SPEC 05-75-0919		SHEET 14 OF 18	
LANTDIV DWS NO			

REVISIONS			
SYM	DESCRIPTION	DATE	APPROVED

SEE PLOT PLAN FOR CONTINUATION

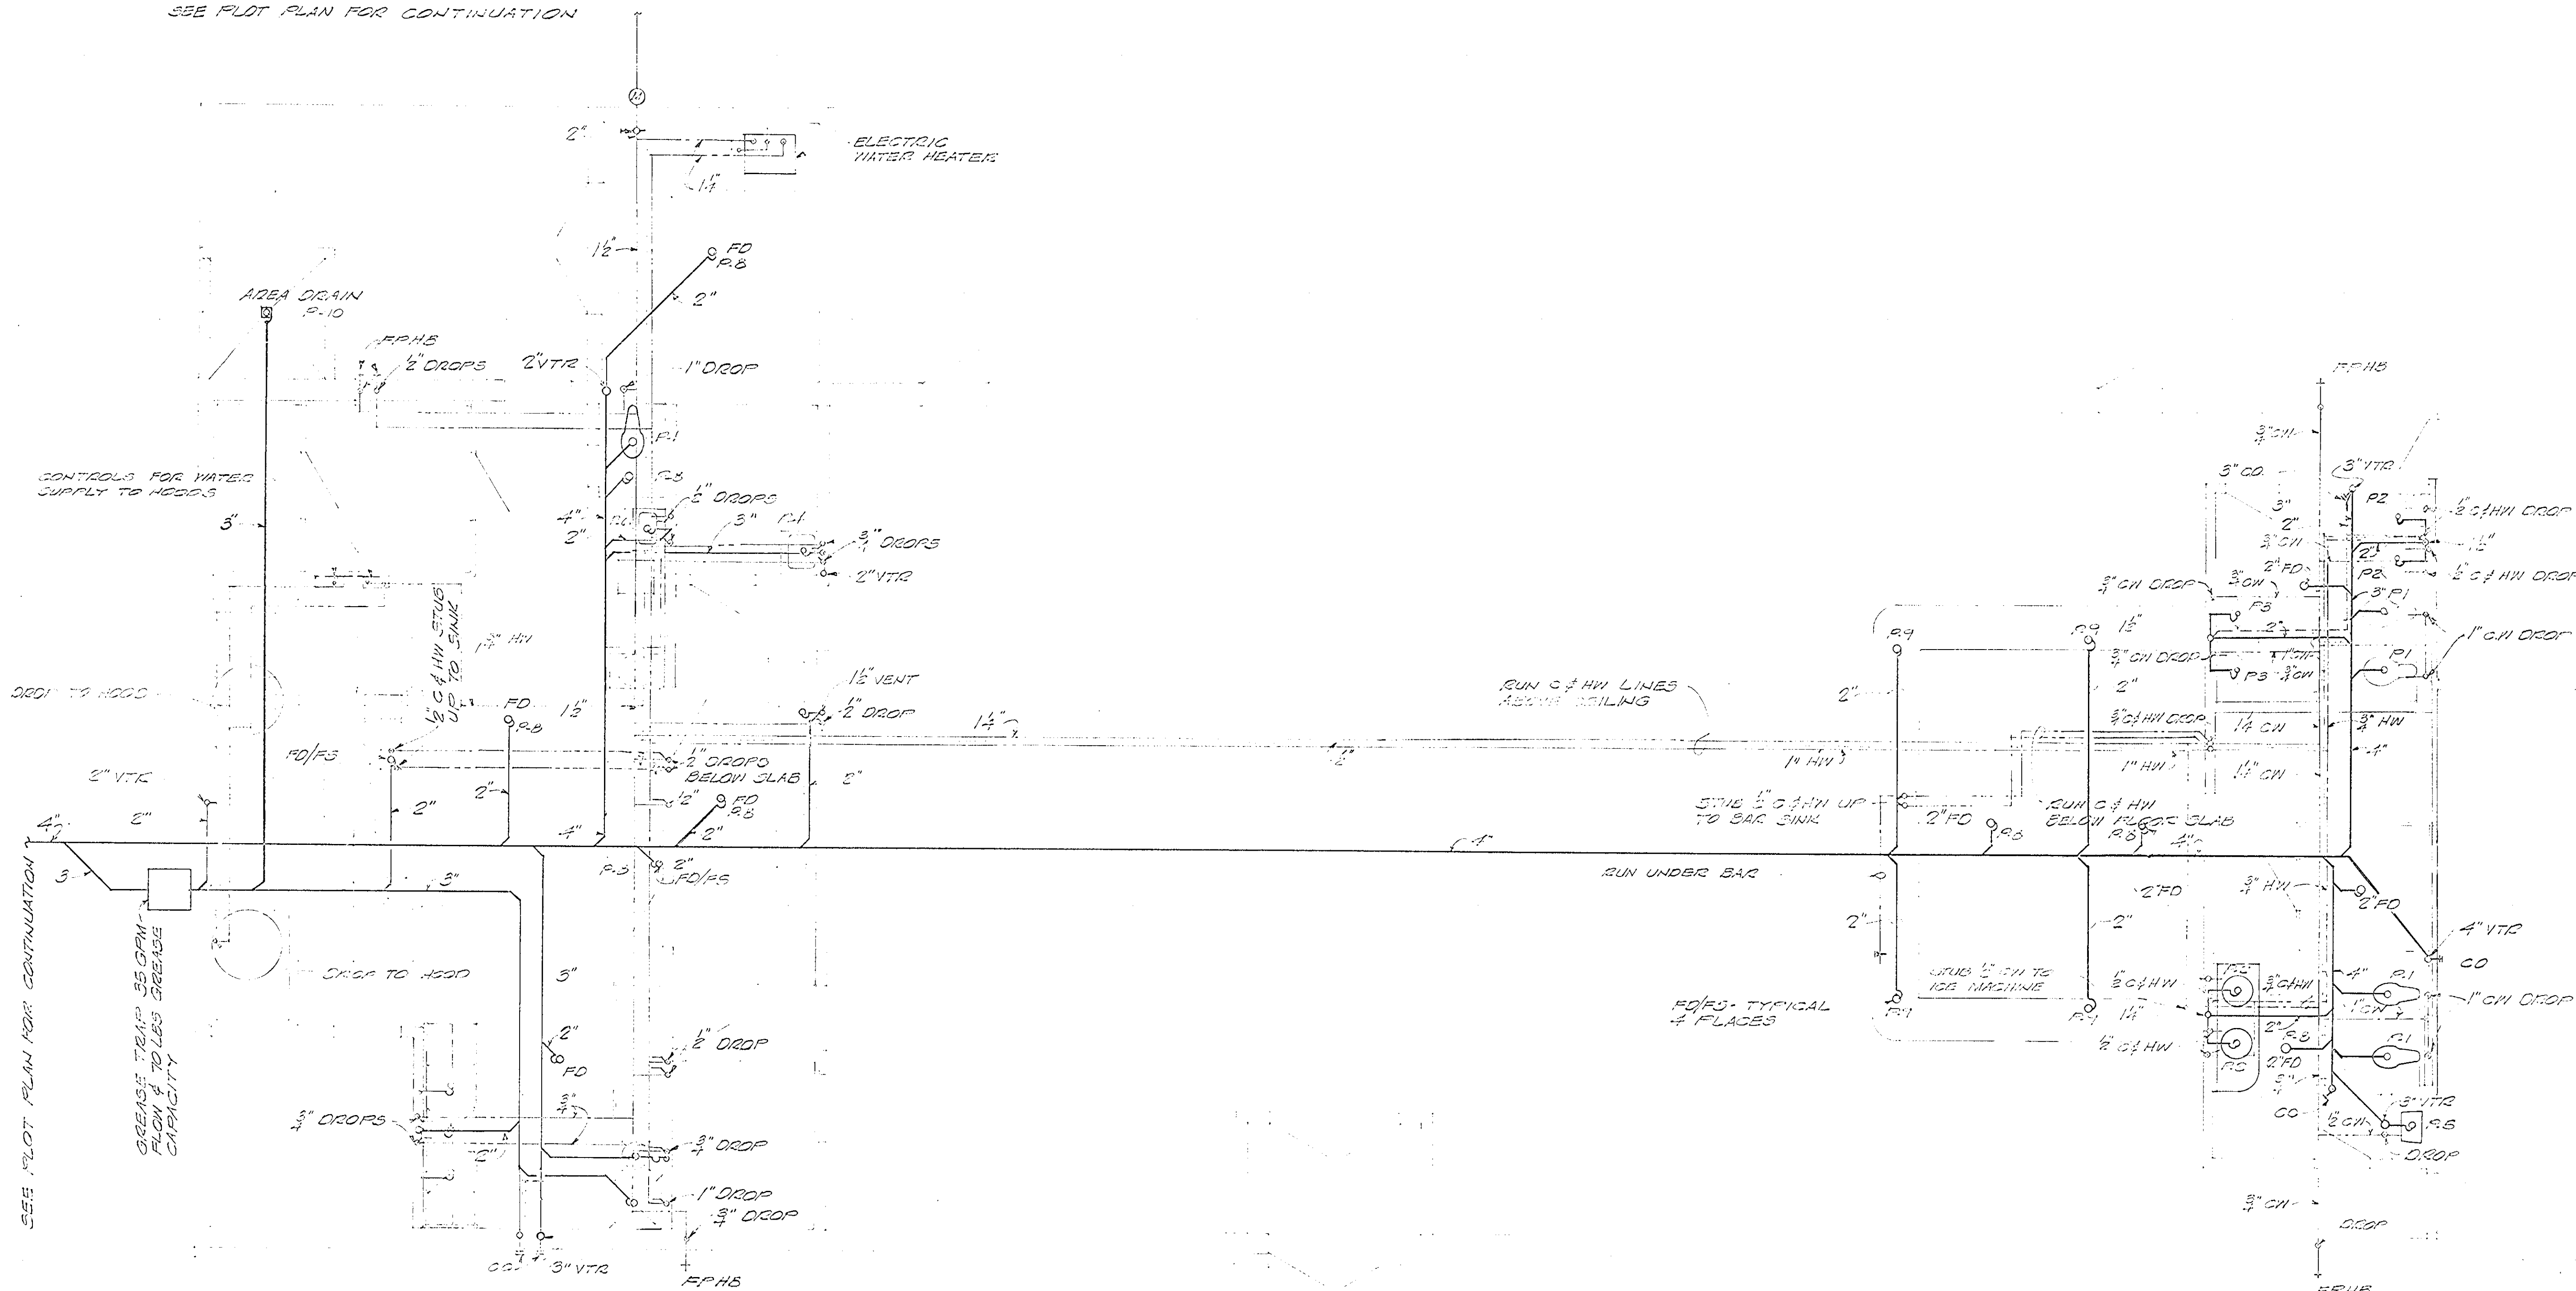

LEGEND

- COLD WATER
HOT WATER
REGULATING LINE
VENT LINE
DRAIN LINE
P.T.C.P
ROOF FROST NOSE BIRD
VENT THRU ROOF
GATE VALVE ON RISER
WATER METER
GATE VALVE


SCHEDULE OF PLUMBING FIXTURE CONNECTIONS					
FIXTURE	DESCRIPTION	CW	MH	DRAIN	REMARKS
P-1	WATER CLOSET	1"	-	2"	
P-2	LAVATORY	3/4"	3/4"	1 1/2"	ROUND & RECTANGULAR
P-3	URINAL	3/4"	-	2"	
P-4	SERVICE SINK	3/4"	3/4"	3"	
P-5	ELECTRIC WATER COOLER	1 1/2"	-	1 1/2"	
P-6	LAVATORY	3/4"	3/4"	1 1/2"	WITH FOOT PEDAL
P-7	LAVATORY	3/4"	3/4"	1 1/2"	SCINTER TOP
P-8	FLOOR DRAIN	-	-	2"	
P-9	FLOOR DRAIN	-	-	2"	WITH FUNNEL STRAINER
P-10	AREA DRAIN	-	-	2"	WITH SEDIMENT BASKET

PLUMBING PLAN SCALE - $\frac{1}{4}" = 1'-0"$

GRAPHIC SCALE



PUBLIC WORKS DEPT. MARINE CORPS BASE CAMP LEJUNE, N.C.		DEPARTMENT OF THE NAVY NAVAL FACILITIES ENGINEERING COMMAND ATLANTIC DIVISION	
DESIGS DR RT CHK CDS PROJMR FGAUJCH ENG 211 APPROVED <i>[Signature]</i> DATE <i>10/2/52</i> PUBLIC WORKS OFFICER SATISFACTORY TO DATE		NAVAL STATION NORFOLK, VIRGINIA MARINE CORPS BASE, CAMP LEJUNE, N.C.	
COMMANDING GENERAL EFD RVD HD DIR APPROVED <i>[Signature]</i> DATE <i>10/2/52</i> FOR COMMANDER, NAVFAC		NCO CLUB, CAMP GEIGER MARINE CORPS BASE, CAMP LEJUNE, N.C. PLUMBING PLAN	
SIZE CODE IDENT NO F 80091		NAVFAC DRAWING NO 4011898 CONSTR CONTR NO N62470-75-B-0919	
SCALE GRAPHIC SPEC 05-75-0919		SHEET 15 OF 18 LANTID DWG NO	

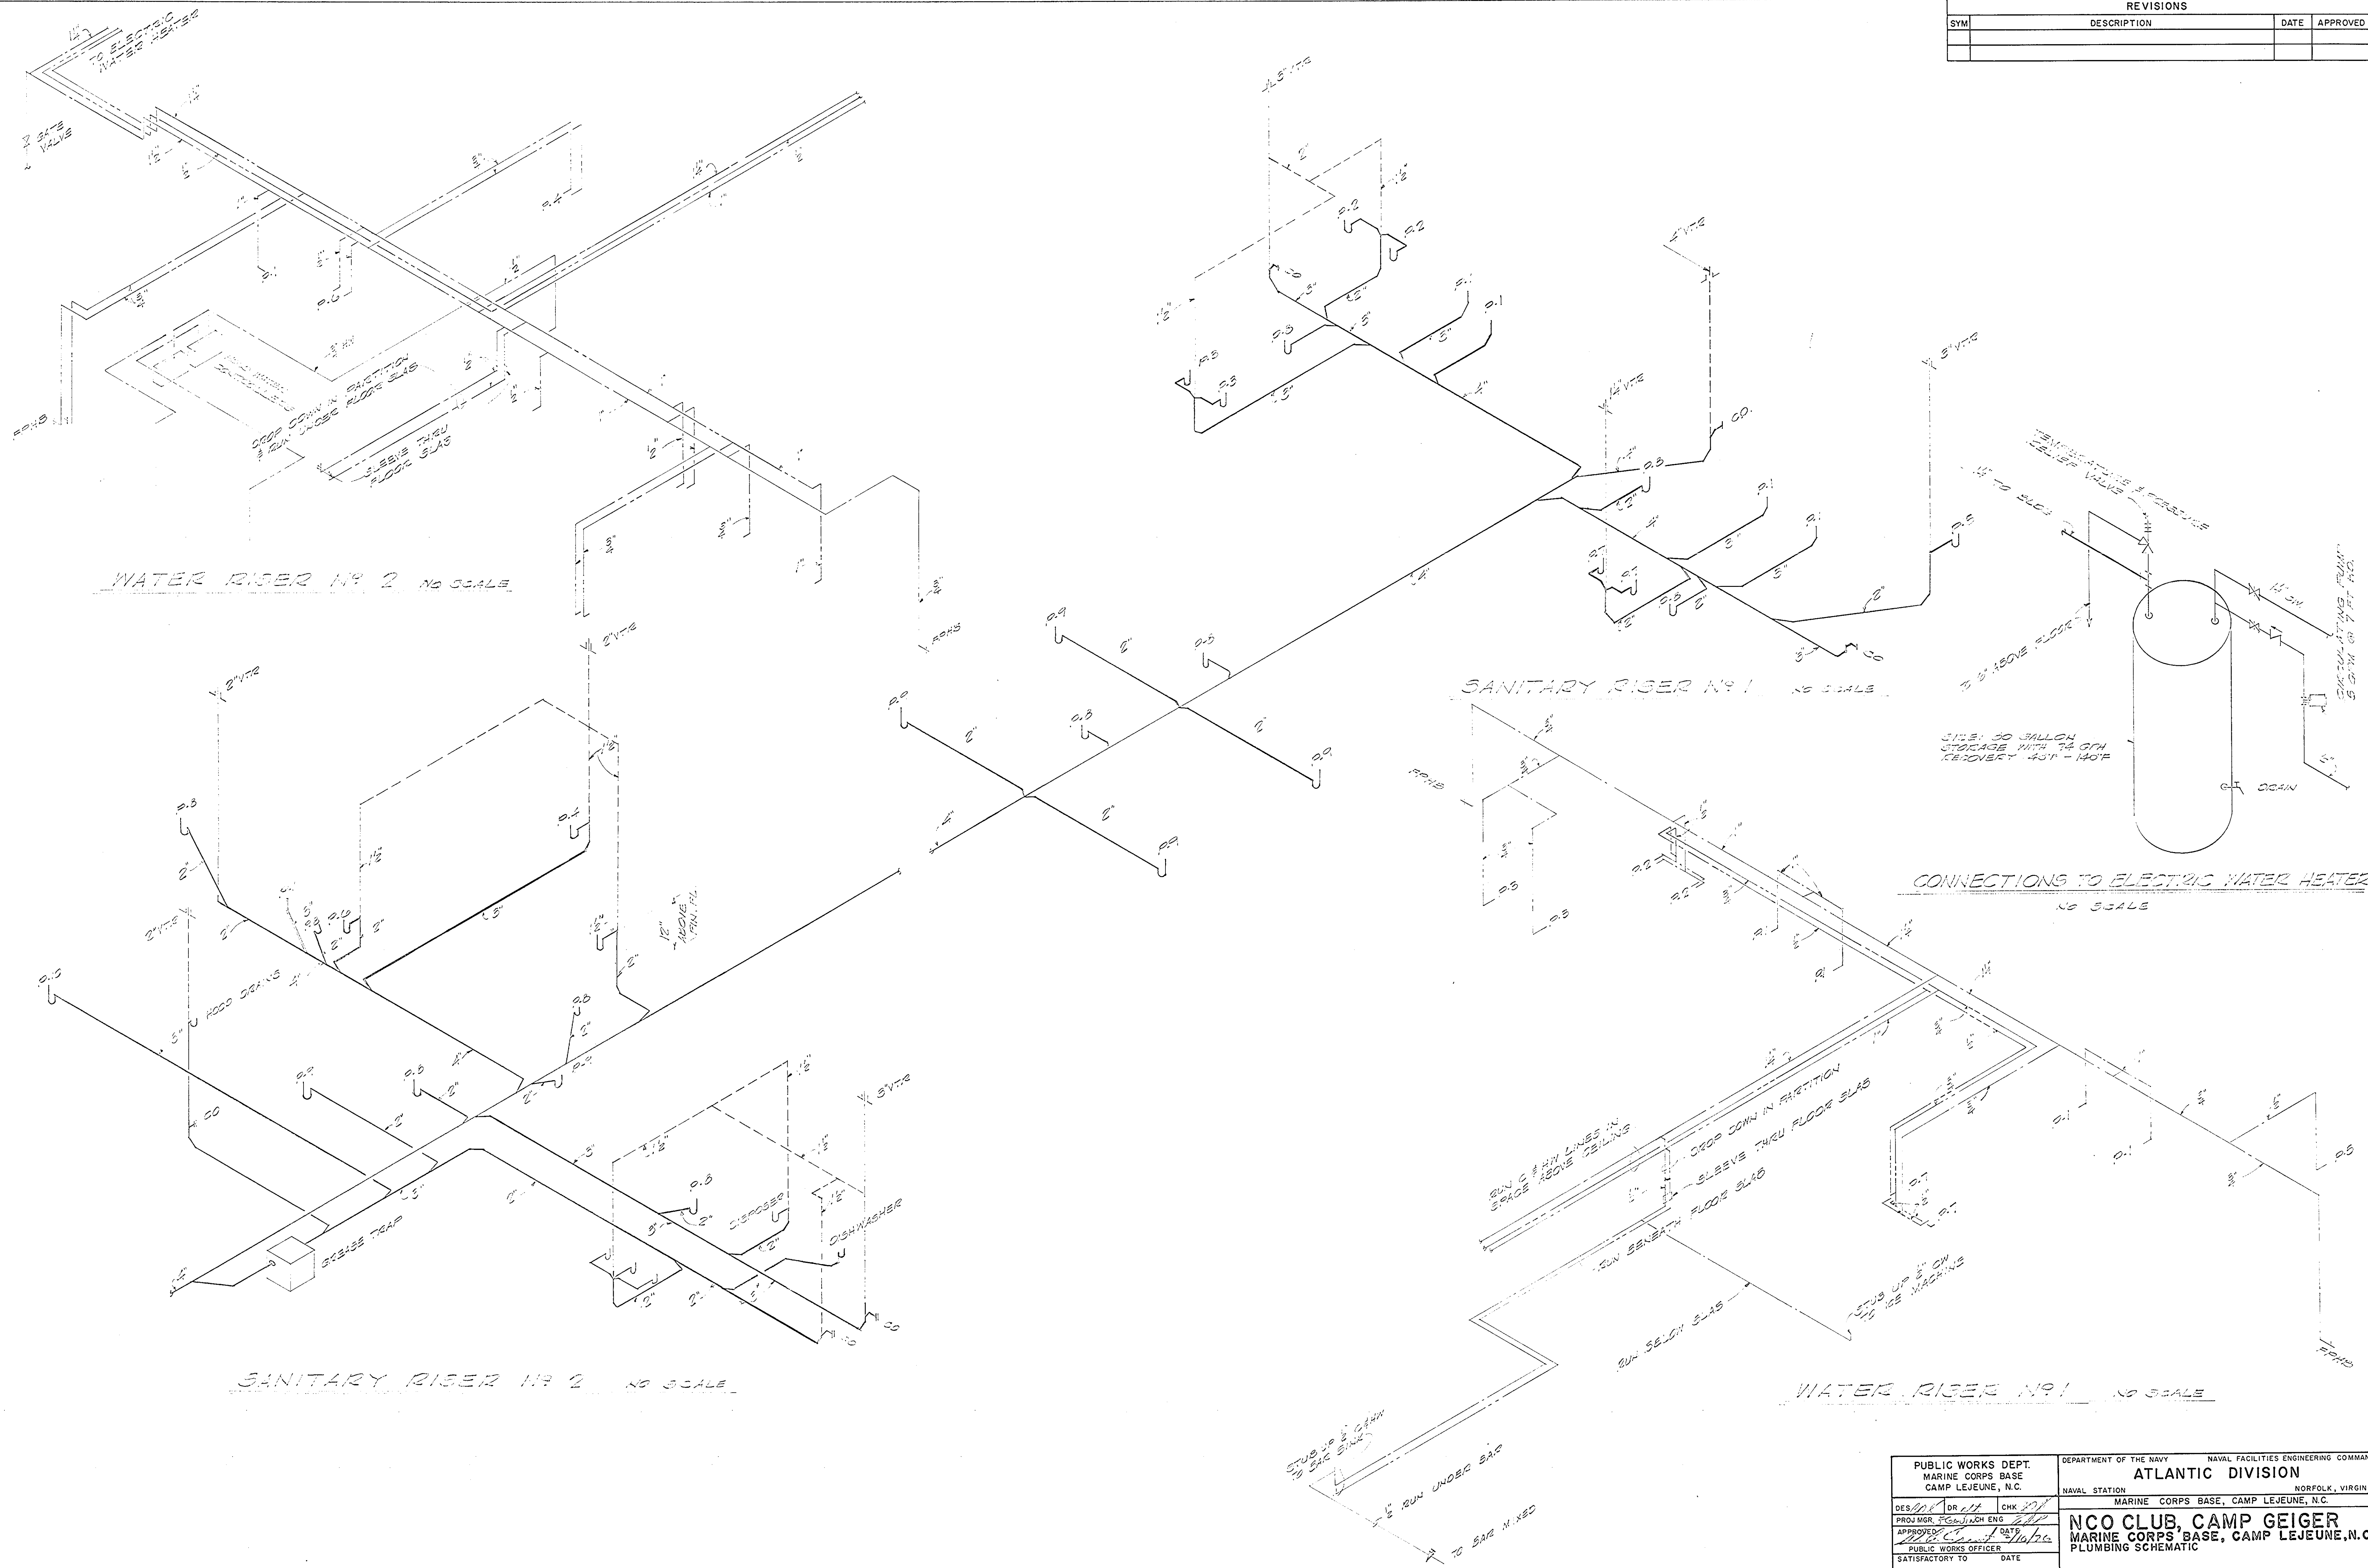

REVISIONS			
SYM	DESCRIPTION	DATE	APPROVED

SATISFACTORY TO
[Signature]
DATE *26 April 76*

PUBLIC WORKS DEPT. MARINE CORPS BASE CAMP LEJEUNE, N.C.		DEPARTMENT OF THE NAVY NAVAL FACILITIES ENGINEERING COMMAND ATLANTIC DIVISION NORFOLK, VIRGINIA	
DESIGNED BY <i>[Signature]</i> OR <i>[Signature]</i> CHK <i>[Signature]</i>		MARINE CORPS BASE, CAMP LEJEUNE, N.C.	
APPROVED BY <i>[Signature]</i> DATE <i>26 April 76</i>		NCO CLUB, CAMP GEIGER MARINE CORPS BASE, CAMP LEJEUNE, N.C.	
Satisfactory to _____		PLUMBING SCHEMATIC	
COMMANDING GENERAL		NAVAC DRAWING NO 401899	
EFD _____ RVD _____		SIZE CODE IDENT NO F 80091	
NO _____ DIR _____		CONSTR CONTR NO N62470-75-B-0919	
APPROVED BY <i>[Signature]</i> DATE _____		SCALE GRAPHIC SPEC 05-75-0919	
FOR COMMANDER, NAVFAC		SHEET 18 OF 18	
		LANTOIV DWG NO	

REVISIONS			
SYM	DESCRIPTION	DATE	APPROVED

PAD MOUNTED TRANSFORMER
225 KVA, 3Ø 12470Δ/120/208Y
WITH PRIMARY FUSES & SECONDARY
BREAKER. PAD SHALL BE 6" STEEL
REINFORCED CONCRETE. PAD SHALL
EXTEND 12' BEYOND TRANSFORMER
ON ALL SIDES. SEE GROUNDING SYSTEM
OF SPECIFICATIONS.

- EXISTING MANHOLE. CONNECT TO EXISTING "2" P.L.C 15KV CABLE FOR POWER SOURCE. CONNECT TO EXISTING 2" 10# EARTH GROUND FOR FIRE ALARM SOURCE.
SEE NAVFAC DRAWING"

4"2/0 TH/ELTW
IN 2" LIQUID TIGHT
FLEXABLE CONDUIT

0 AMP.

FATIO

EMERGENCY LIGHTING CONSOLE
-SEE SPECIFICATIONS

4"4THW&1"8TW)
IN 1-1/4" FLEXABLE
CONDUIT.

12" 12 THW IN 3/4"
CONDUIT. (CONTROL
CIRCUITS FOR EXHAUST
SYSTEM OVER COOKING
AREA.

MOUNTED ON ROOF

STUB-UP&CONNECT
TO FF-5

ELECTRIC PLAN
SCALE 1/4" = 1'-0"

2-HOLE COVER W/GASKET →

PHOTOELECTRIC
CONTROL _____

300 WATT PAR 56
FLOOD LAMP

~~DIE-CAST ALUMINUM, CORROSION &
WEATHER PROOF FIXTURE WITH
SWIVEL ARM~~

DETAIL "C"
NO SCALE

NOTES

EF-1-2&ETC INDICATE EXHAUST FANS AS SHOWN
ON NAVFAC DRAWING #4011895

ALL JUNCTION BOXES, OUTLETS ETC. SHALL BE
LOCATED IN COORDINATION WITH AND COMPATIBLE
TO EQUIPMENT SERVED.

NOTE "A"
MOTORIZED LOUVER IN GABEL END. RUN (2) 1/2" TW
IN 1/2" CONDUIT BACK TO LOAD SIDE OF THERMOSTAT
CONTROLLING EF-3. CONNECT IN PARALLEL WITH
EF-3.

GRAPHIC SCALE

PUBLIC WORKS DEPT. MARINE CORPS BASE CAMP LEJUNE, N.C.		DEPARTMENT OF THE NAVY NAVAL FACILITIES ENGINEERING COMMAND ATLANTIC DIVISION	
DES <u>101</u> DR <u>101</u> CNK <u>101</u> NO. 101 MC. CH ENG.		NAVAL STATION NORFOLK, VIRGINIA MARINE CORPS BASE, CAMP LEJUNE, N.C.	
APPROVED <u>101</u> DATE <u>10/10/58</u> PUBLIC WORKS OFFICER		NCO CLUB, CAMP GEIGER MARINE CORPS BASE, CAMP LEJUNE, N.C.	
SATISFACTORY TO DATE		ELECTRICAL PLAN, LEGEND, DETAILS & SECTIONS	
COMMANDING GENERAL EFO RVD ND DIR		SIZE CODE IDENT NO NAVAFAC DRAWING NO 4011900	
APPROVED <u>101</u> DATE <u>10/10/58</u> FOR COMMANDER, NAVAFAC		F 80091 CONSTR CONTR NO N62470-75-B-01919	
SCALE GRAPHIC		SPEC 05-75-0919	
SHEET 17 OF 18		LANTDIV DWG NO	

SATISFACTORY TO

DATE 26 April 76

POWER & APPLIANCE PANEL "PA" SCHEDULE

CIRCUIT	CIRCUIT BREAKER	WIRE AND CONDUIT	SERVING
NUMBER	POLE	SIZE	CLASS
1	1	20A	2 1/2" TW 1/2"
2	"	"	"
3	"	"	"
4	"	"	"
5	"	"	"
6	"	"	"
7	"	"	"
8	"	30A	2 1/2" TW GR. 1/2"
9	"	35A	2 1/2" TW GR. 3/4"
10	2	30A	2 1/2" TW GR. 1/2"
11	2	15A	2 1/2" TW GR. 1"
12	3	20A	2 1/2" TW GR. 1/2"
13	3	20A	2 1/2" TW GR. 1/2"
14	3	20A	2 1/2" TW GR. 1/2"
15	3	20A	2 1/2" TW GR. 1/2"
16	3	30A	2 1/2" TW GR. 3/4"
17	3	70A	2 1/2" TW GR. 1-1/4"
18	3	70A	2 1/2" TW GR. 1-1/4"
19	3	170A	2 1/2" TW GR. 2"
20	3	100A	2 1/2" TW GR. 1-1/2"

MAIN PANEL "M P" SCHEDULE

CIRCUIT BREAKER				WIRE AND CONDUIT SIZE		SERVING	
CIRCUIT NUMBER	POLE	SIZE	CLASS				
1	1	20A	15	1"12 TW GR. 2"12 THW	1/2"	LIGHTING	
2	"	"	"	"	"	"	
3	"	"	"	"	"	"	
4	"	"	"	"	"	"	
5	"	"	"	"	"	"	
6	"	"	"	"	"	"	
7	"	"	"	"	"	"	
8	"	"	"	"	"	"	
9	"	"	"	"	"	"	
10	"	"	"	"	"	"	
11	"	"	"	"	"	EMERGENCY LIGHTING CONSOLE	
12	"	"	"	"	"	SPARE	
13	"	"	"	1"12 TW GR. 2"12 THW	1/2"	WALK-IN REFRIGERATOR & FREEZER LIGHTING	
14	"	"	"	"	"	CONVENIENCE OUTLETS	
15	"	"	"	"	"	"	
16	"	"	"	"	"	"	
17	"	"	"	"	"	"	
18	"	"	"	"	"	"	
19	"	"	"	"	"	"	
20	"	"	"	"	"	"	
21	"	"	"	"	"	"	
22	2	25A	20	1"12 TW GR. 2"10 THW	"	TOASTERS	
23	2	100A	20	1"8 TW GR. 2"10 THW	1-1/2"	HOT WATER HEATER	
24	3	50A	20	1"10 TW 3"6 THW	"	DEEP FAT FRIER	
25	3	50A	20	"	"	"	
26	3	50A	20	"	"	GRIDDLE	
27	3	80A	20	1"8 TW 3"4 THW	1 1/4"	HOT TOP RANGE	
28	3	400A	4b	1"2 TW 8"300 MCM THW	4"	PANEL "PA"	

[illegible]

PUBLIC WORKS DEPT. MARINE CORPS BASE CAMP LEJEUNE, N.C.			NAVAL FACILITIES ENGINEERING COMMAND ATLANTIC DIVISION		
DES <u>187</u> DR <u>101</u> CHK <u>221</u>			NAVAL STATION		NORFOLK, VIRGINIA
PROJ MOR <u>2</u> CIVIL ENG <u>224</u> APPROVED _____ DATE <u>10/1/54</u> <u>W. E. Brown</u>			MARINE CORPS BASE, CAMP LEJEUNE, N.C.		
PUBLIC WORKS OFFICER			NCO CLUB, CAMP GEIGER MARINE CORPS BASE, CAMP LEJEUNE, N.C. ELECTRICAL PANEL SCHEDULE		
SATISFACTORY TO _____ DATE _____					
COMMANDING GENERAL			SIZE CODE IDENT NO		
EFD _____ RVD _____			F 80091		NAVFAC DRAWING NO 401901
HD _____ DIR _____					CONSTR CONTR NO N62470-75-B-0919
APPROVED _____ DATE <u>10/1/54</u> <u>W. E. Brown</u>			SCALE GRAPHIC		SPEC 05-75-0919
FOR COMMANDER, NAVFAC					SHEET 18 OF 18
SATISFACTORY TO <u>W. E. Brown</u>			LANTRIV DWG NO _____		
DATE <u>26 April 76</u>					