


SHEET INDEX			
SEQ	NAVFAC DRAWING NO.	NO	DRAWING TITLE
STRUCTURAL			
254	17361877	S-001	STRUCTURAL GENERAL NOTES
255	17361878	S-002	STRUCTURAL GENERAL NOTES
256	17361879	S-101	FOUNDATION PLANS
257	17361880	S-501	TYPICAL CONCRETE DETAILS
258	17361881	S-502	TYPICAL CONCRETE DETAILS
259	17361882	S-503	CONCRETE SECTIONS AND DETAILS
ARCHITECTURAL			
260	17361883	A-001	GENERAL NOTES, SYMBOLS, AND EXTERIOR PERSPECTIVE VIEWS
261	17361884	A-406	DETACHED EQUIPMENT YARD
ELECTRICAL			
262	17361885	E-001	ELECTRICAL LEGEND 1 OF 2
263	17361886	E-002	ELECTRICAL LEGEND 2 OF 2
264	17361887	ED101	ELECTRICAL DEMOLITION PLAN 1
265	17361888	ED102	ELECTRICAL DEMOLITION PLAN 2
266	17361889	ED601	EXISTING DISTRIBUTION ONE LINE DIAGRAM - DEMOLITION PLAN
267	17361890	ES101	ELECTRICAL SITE PLAN 1
268	17361891	ES102	ELECTRICAL SITE PLAN 2
269	17361892	ES103	ELECTRICAL SITE PLAN 3
270	17361893	ES104	ELECTRICAL SITE PLAN 4
271	17361894	ES105	ELECTRICAL SITE PLAN 5
272	17361895	ES201	ELECTRICAL ELEVATIONS - BLDG. A
273	17361896	ES501	ELECTRICAL SITE DETAILS
274	17361897	ES502	ELECTRICAL SITE DETAILS
275	17361898	ES503	ELECTRICAL SITE DETAILS
276	17361899	ES504	ELECTRICAL SITE DETAILS
277	17361900	ES505	ELECTRICAL SITE DETAILS
278	17361901	ES506	ELECTRICAL SITE DETAILS
279	17361902	ES701	HIGH MAST LIGHT POLE LOCATIONS
280	17361903	EP601	EXISTING DISTRIBUTION ONE LINE DIAGRAM - NEW WORK
281	17361904	EP602	ONE-LINE DIAGRAMS
282	17361905	EP701	PANELBOARD SCHEDULES
283	17361906	EA101	AIRFIELD ELECTRICAL PLAN 1
284	17361907	EA102	AIRFIELD ELECTRICAL PLAN 2
285	17361908	EA501	AIRFIELD LIGHTING DETAILS
286	17361909	EA502	AIRFIELD LIGHTING DETAILS
287	17361910	EA503	AIRFIELD LIGHTING DETAILS
288	17361911	EA504	AIRFIELD LIGHTING DETAILS
289	17361912	EA701	AIRFIELD LIGHTING POINTS SCHEDULE
290	17361913	EA702	AIRFIELD LIGHTING ONE-LINE DIAGRAMS
TELECOMM			
291	17361914	TS001	TELECOMMUNICATIONS SITE LEGEND
292	17361915	TD101	TELECOMMUNICATIONS SITE DEMOLITION PLAN 1
293	17361916	TD102	TELECOMMUNICATIONS SITE DEMOLITION PLAN 2
294	17361917	TS101	TELECOMMUNICATIONS SITE PLAN 1
295	17361918	TS102	TELECOMMUNICATIONS SITE PLAN 2
296	17361919	TS103	TELECOMMUNICATIONS SITE PLAN 3
297	17361920	TS104	TELECOMMUNICATIONS SITE PLAN 4
298	17361921	TS105	TELECOMMUNICATIONS SITE PLAN 5
298.1	17362001	TS106	TELECOMMUNICATIONS SITE PLAN 6
298.2	17362002	TS107	TELECOMMUNICATIONS SITE PLAN 7
298.3	17362003	TS108	TELECOMMUNICATIONS SITE PLAN 8
298.4	17362004	TS109	TELECOMMUNICATIONS SITE PLAN 9
298.5	17361922	TS601	TELECOMMUNICATIONS SITE DETAILS
299	17361923	TS502	TELECOMMUNICATIONS SITE DETAILS
300	17361924	TS701	TELECOMMUNICATIONS INTERBUILDING BACKBONE RISER

SHEET INDEX			
SEQ	NAVFAC DRAWING NO.	NO	DRAWING TITLE
FUELS - CIVIL			
302	17361925	CF101	OVERALL FUELING PLAN
303	17361926	CF102	OVERALL COMM PLAN
304	17361927	CF201	FUEL PLAN AND PROFILE - AREA 1
305	17361928	CF202	FUEL PLAN AND PROFILE - AREA 2
306	17361929	CF203	FUEL PLAN AND PROFILE - AREA 3
307	17361930	CF204	FUEL PLAN AND PROFILE - AREA 4
308	17361931	CF205	FUEL PLAN AND PROFILE - AREA 5
309	17361932	CF206	FUEL PLAN AND PROFILE - AREA 6
310	17361933	CF207	FUEL PLAN AND PROFILE - AREA 7
311	17361934	CF208	FUEL PLAN AND PROFILE - AREA 8
312	17361935	CF209	FUEL PLAN AND PROFILE - AREA 9
313	17361936	CF210	FUEL PLAN AND PROFILE - AREA 10
314	17361937	CF211	FUEL PLAN AND PROFILE - AREA 11
315	17361938	CF212	FUEL PLAN AND PROFILE - AREA 12
316	17361939	CF221	COMM PLAN - AREA 1
317	17361940	CF222	COMM PLAN - AREA 2
318	17361941	CF223	COMM PLAN - AREA 3
319	17361942	CF224	COMM PLAN - AREA 4
320	17361943	CF225	COMM PLAN - AREA 5
321	17361944	CF226	COMM PLAN - AREA 6
322	17361945	CF227	COMM PLAN - AREA 7
323	17361946	CF228	COMM PLAN - AREA 8
324	17361947	CF229	COMM PLAN - AREA 9
325	17361948	CF230	COMM PLAN - AREA 10
326	17361949	CF231	COMM PLAN - AREA 11
327	17361950	CF232	COMM PLAN - AREA 12
328	17361951	CF233	COMM PLAN - AREA 13
329	17361952	CF234	COMM PLAN - AREA 14
330	17361953	CF501	FUELING DETAILS
331	17361954	CF502	FUELING DETAILS
FUELS - STRUCTURAL			
332	17361955	SF001	STRUCTURAL GENERAL NOTES - SHEET 1
333	17361956	SF002	STRUCTURAL GENERAL NOTES - SHEET 2
334	17361957	SF003	LEGENDS AND ABBREVIATIONS
335	17361958	SF101	OVERALL STRUCTURAL LAYOUT
336	17361959	SF111	ISOLATION VALVE VAULT 1 - PLANS
337	17361960	SF112	ISOLATION VALVE VAULT 2 - PLANS - SHEET 1
338	17361961	SF113	ISOLATION VALVE VAULT 2 - PLAN - SHEET 2
339	17361962	SF114	HYDRANT PIT - PLANS AND SECTIONS
340	17361963	SF115	HPV PITS - PLANS AND SECTIONS
341	17361964	SF501	STANDARD STRUCTURAL DETAILS - SHEET 1
342	17361965	SF502	STANDARD STRUCTURAL DETAILS - SHEET 2
343	17361966	SF511	ISOLATION VALVE VAULT - SECTIONS - SHEET 1
344	17361967	SF512	ISOLATION VALVE VAULT - SECTIONS - SHEET 2
345	17361968	SF513	ISOLATION VALVE VAULT - SECTIONS AND DETAILS
346	17361969	SF521	ROLLING COVER - SHEET 1
347	17361970	SF522	ROLLING COVER - SHEET 2
348	17361971	SF523	ROLLING COVER - SHEET 3
349	17361972	SF524	ROLLING COVER - SHEET 4
350	17361973	SF525	ROLLING COVER - SHEET 5
351	17361974	SF551	PIPE SUPPORT DETAILS
FUELS - MECHANICAL			
352	17361975	MF001	FUELING MECHANICAL LEGEND
353	17361976	MF002	FUELING MECHANICAL GENERAL NOTES
354	17361977	MF011	FUELING MECHANICAL FLOW DIAGRAM - OVERALL
355	17361978	MF101	FUELING MECHANICAL OVERALL SITE PLAN
356	17361979	MF501	FUELING MECHANICAL DETAILS - ISOLATION VALVE VAULT (IVV-1)
357	17361980	MF502	FUELING MECHANICAL DETAILS - ISOLATION VALVE VAULT (IVV-2)
358	17361981	MF503	FUELING MECHANICAL DETAILS - ISOLATION VALVE VAULT (IVV-2)
359	17361982	MF504	FUELING MECHANICAL DETAILS
360	17361983	MF505	FUELING MECHANICAL DETAILS
361	17361984	MF506	FUELING MECHANICAL DETAILS
362	17361985	MF601	FUELING MECHANICAL P&ID
FUELS - ELECTRICAL			
363	17361986	EF001	ELECTRICAL FUELING LEGEND - 1
364	17361987	EF002	ELECTRICAL FUELING LEGEND - 2
365	17361988	EF011	OVERALL FUELING HAZARDOUS AREA PLAN
366	17361989	EF101	OVERALL FUELING ELECTRICAL SITE PLAN
367	17361990	EF401	ENLARGED PLAN - PUMPHOUSE
368	17361991	EF501	ELECTRICAL DETAILS - EPDS
369	17361992	EF502	ELECTRICAL DETAILS - GROUNDING
370	17361993	EF503	ELECTRICAL SITE DETAILS - HANDHOLES
371	17361994	EF504	ELECTRICAL SITE DETAILS - DUCT BANKS
372	17361995	EF511	ELEVATION - PUMP CONTROL PANEL
373	17361996	EF611	PCP - CONTROL DIAGRAM
374	17361997	EF621	NORTH APRON EPDS - FRONT LAYOUT
375	17361998	EF622	NORTH ARON EPDS WIRING - 1
CATHODIC PROTECTION			
376	17361999	EK501	CATHODIC PROTECTION DETAILS
377	17362000	EK502	CATHODIC PROTECTION DETAILS

[illegible]

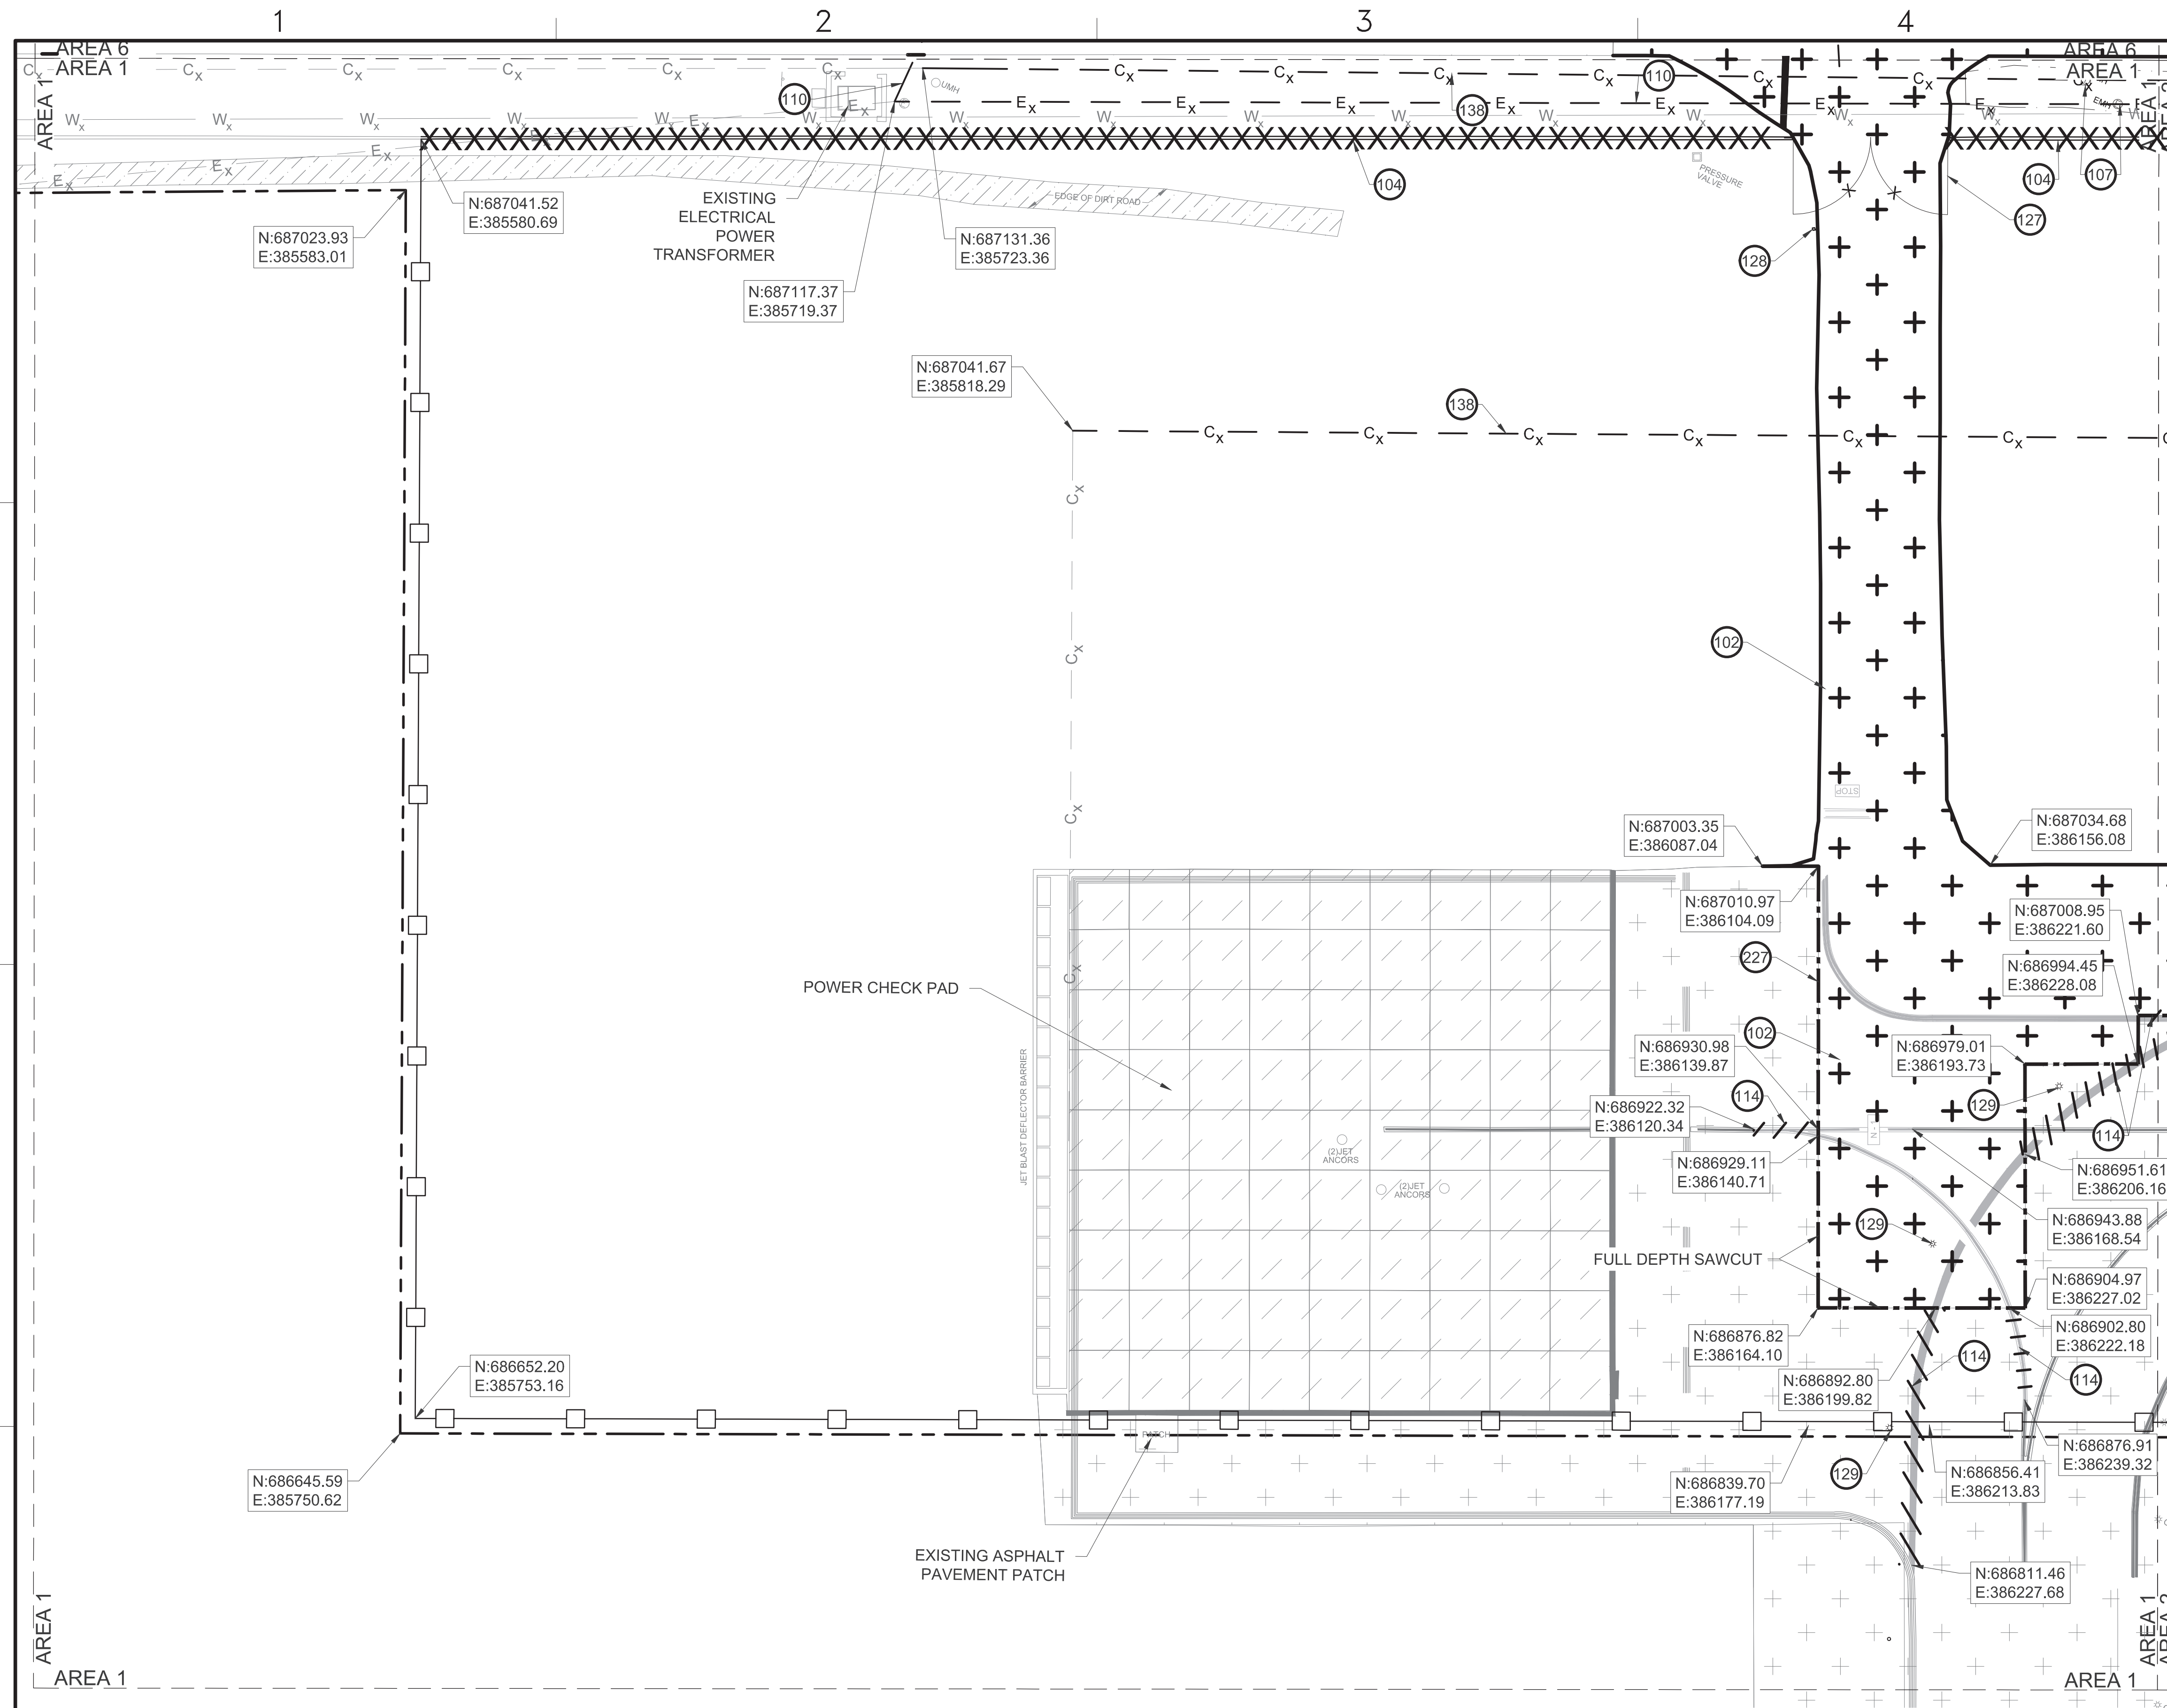

GENERAL NOTES


- | | |
|---|--|
| A | EXISTING IMPROVEMENTS NOT SHOWN REMOVED ON DEMOLITION PLAN SHEETS MUST BE PROTECTED IN PLACE. |
| B | SAW CUT A STRAIGHT EDGE ALONG EXISTING ASPHALT PAVEMENT FOR INSTALLATION OF NEW PAVEMENT. |
| C | PROTECT EXISTING EDGES OF PAVEMENT TO REMAIN. |
| D | EXISTING SECURITY FENCE MUST REMAIN IN PLACE UNTIL TEMPORARY OR PERMANENT FENCING IS INSTALLED AND ACCEPTED. THE AIRFIELD MUST BE SECURE AT ALL TIMES. |
| E | COMPLY WITH ENVIRONMENTAL REQUIREMENTS AND REGULATIONS. REFER TO DIVISIONS 01 AND 02 SPECIFICATIONS. |
| F | FOR BIDDING PURPOSES, ASSUME THE THICKNESS OF THE EXISTING ASPHALT IS 6-INCHES. |

KEYNOTES

102	REMOVE EXISTING ASPHALT PAVEMENT
104	REMOVE EXISTING CONCRETE WALL
107	REMOVE EXISTING ELECTRICAL MANHOLE
110	REMOVE EXISTING UNDERGROUND ELECTRIC, RE: ED101 & ED102
114	REMOVE EXISTING PAVEMENT MARKING
127	REMOVE EXISTING GATE
128	REMOVE EXISTING GATE KEYPAD AND ASSOCIATED CABLE/CONDUIT
129	REMOVE EXISTING TAXIWAY EDGE LIGHT AND REPLACE WITH BLANK COVERS, RE: ED101
138	REMOVE EXISTING UNDERGROUND COMM LINE, RE: TD101 & TD102
227	RECONSTRUCT EXIST ASPHALT EDGE BEFORE TYING INTO NEW PAVEMENT EDGE, RE: A3/CS502

LEGEND

	REMOVE ASPHALT PAVEMENT
	EXISTING CONCRETE PAVEMENT TO REMAIN
	EXISTING ASPHALT PAVEMENT TO REMAIN
	EXISTING DIRT ROAD
	LIMITS OF DISTURBANCE
	REMOVE EXISTING CONCRETE WALL
	REMOVE EXISTING PAVEMENT MARKING
	FULL DEPTH SAWCUT
	REMOVE EXISTING UNDERGROUND COMM LINE, RE: TD101 & TD102
	REMOVE EXISTING UNDERGROUND ELECTRIC, RE: ED101 & ED102
	EXISTING CONCRETE WALL TO REMAIN
	EXISTING WATERLINE TO REMAIN
	EXISTING UNDERGROUND ELECTRIC TO REMAIN
	EXISTING PAVEMENT MARKING TO REMAIN
	EXISTING UNDERGROUND COMM LINE TO REMAIN
	TEMPORARY FENCE (FREE ZONE BOUNDARY), RE: A1/CS006

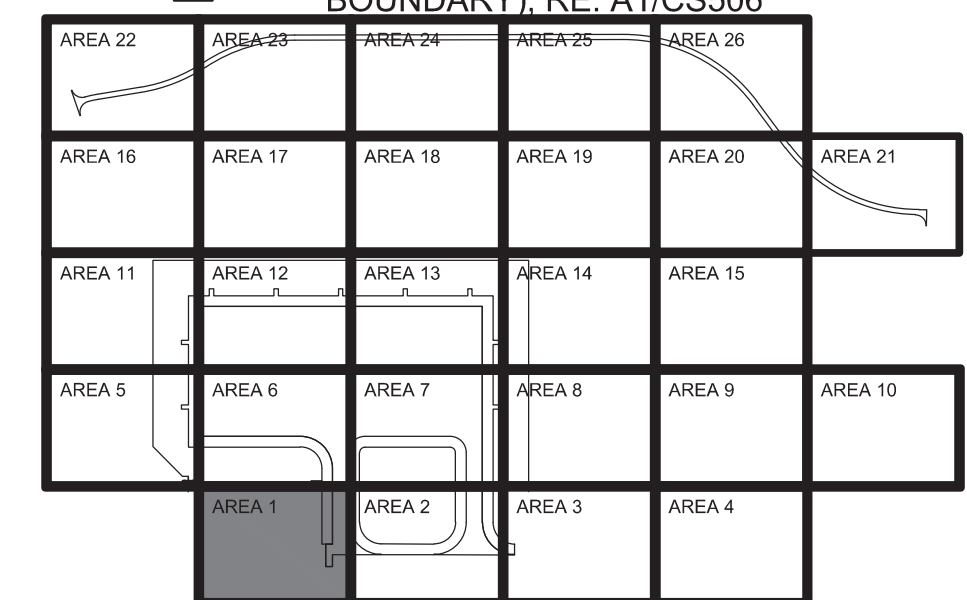


AREA 1 KEY PLAN

GRAPHIC SCALE



SCALE 411001

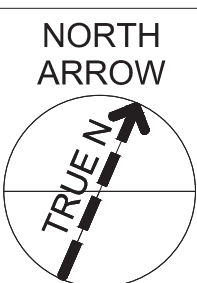

SCALE: AS SHOWN

PROJECTS NO.: 1665555

AVFAC DRAWING NO.
17261682


17361682

SHEET 59 OF 377

CD102

IF SHEET IS LESS THAN 22" X 34"
REDUCED PRINT. USE GRAPHIC SCALES


FILE NAME: U:\BLDG NAVFAC Pacific\03430603 - P-012 North Aircraft Parking Ramp\700 Working Documents\740 Sheets\740.01 Civil\0102_1665555_CD104.dwg
LAYOUT NAME: DEMOLITION PLAN - AREA 3
PLOTED: 03/16/2026 7:05pm
USER: CameroS

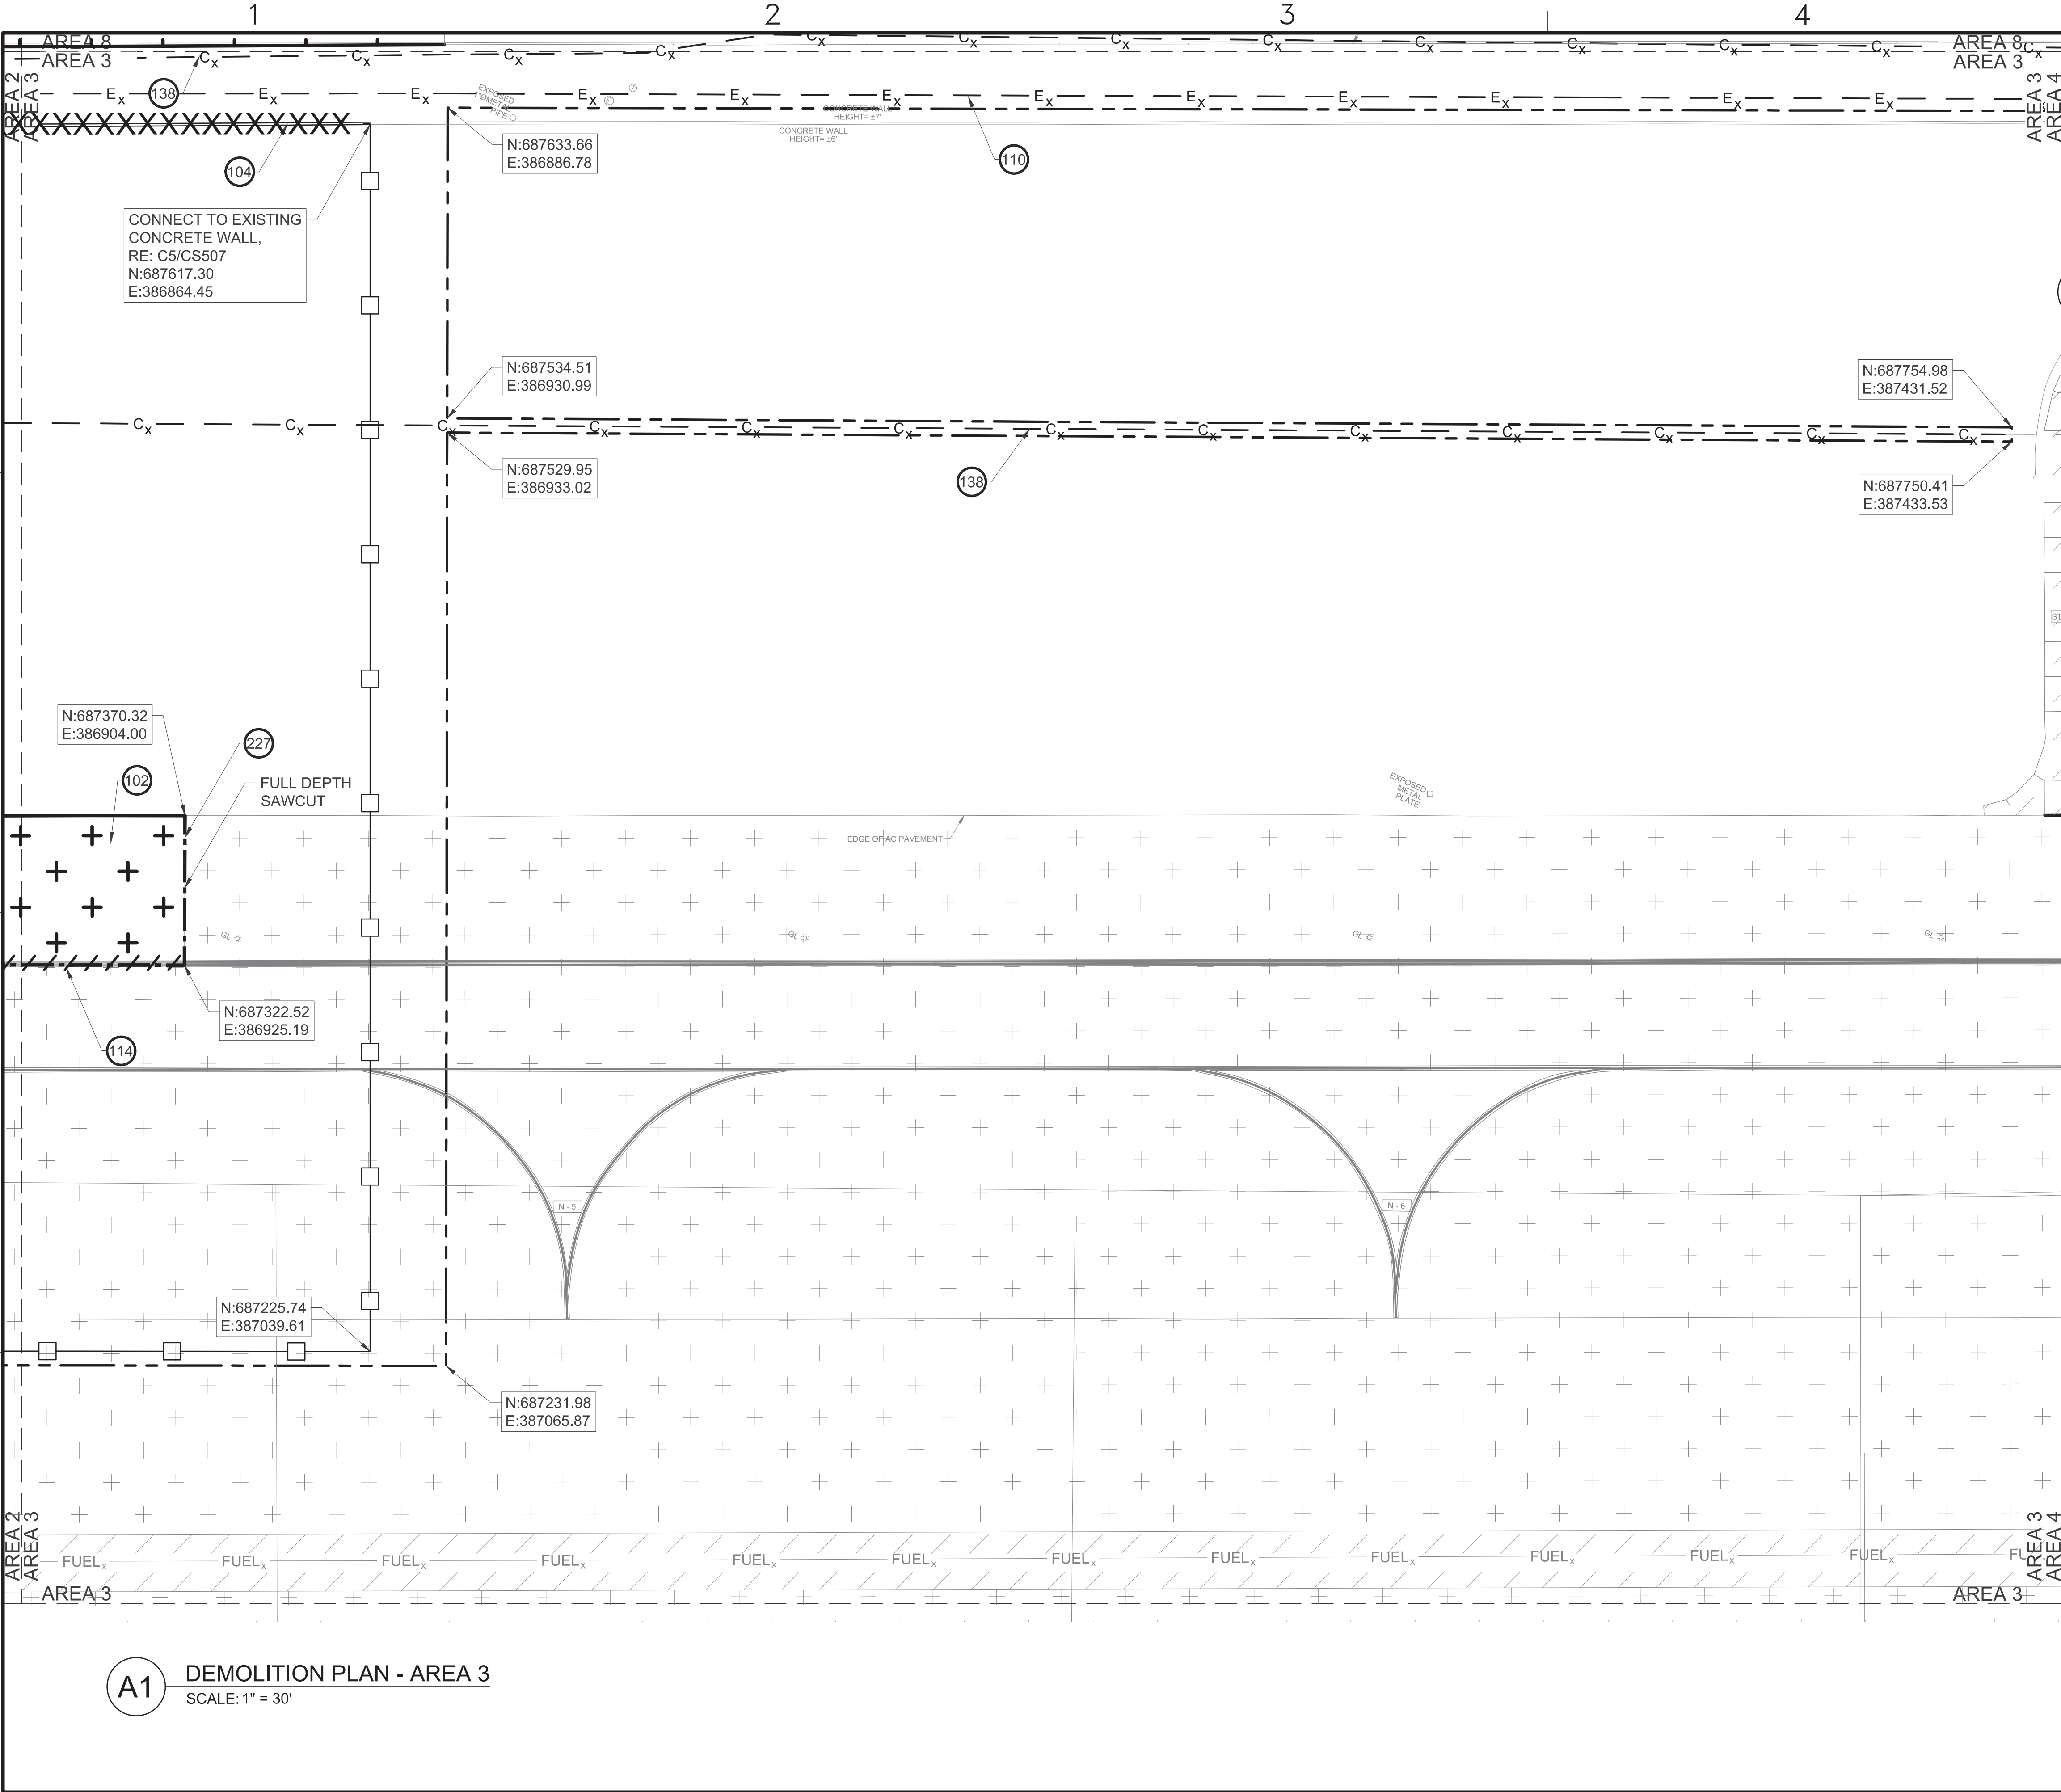

GENERAL NOTES	
A	EXISTING IMPROVEMENTS NOT SHOWN REMOVED ON DEMOLITION PLAN SHEETS MUST BE PROTECTED IN PLACE.
B	CUT A STRAIGHT EDGE ALONG EXISTING ASPHALT PAVEMENT FOR INSTALLATION OF NEW PAVEMENT.
C	PROTECT EXISTING EDGES OF PAVEMENT TO REMAIN.
D	EXISTING SECURITY FENCE MUST REMAIN IN PLACE UNTIL TEMPORARY OR PERMANENT FENCING IS INSTALLED AND ACCEPTED. THE AIRFIELD MUST BE SECURE AT ALL TIMES.
E	COMPLY WITH ENVIRONMENTAL REQUIREMENTS AND REGULATIONS. REFER TO DIVISIONS 01 AND 02 SPECIFICATIONS.
F	FOR BIDDING PURPOSES, ASSUME THE THICKNESS OF THE EXISTING ASPHALT IS 6-INCHES.

KEYNOTES	
102	REMOVE EXISTING ASPHALT PAVEMENT
104	REMOVE EXISTING CONCRETE WALL
110	REMOVE EXISTING UNDERGROUND ELECTRIC, RE: ED101 & ED102
114	REMOVE EXISTING PAVEMENT MARKING
138	REMOVE EXISTING UNDERGROUND COMM LINE, RE: TD101 & TD102
227	RECONSTRUCT EXIST ASPHALT EDGE BEFORE TYING INTO NEW PAVEMENT EDGE, RE: A3/CS502

LEGEND	
	REMOVE ASPHALT PAVEMENT
	EXISTING CONCRETE PAVEMENT TO REMAIN
	EXISTING ASPHALT PAVEMENT TO REMAIN
	LIMITS OF DISTURBANCE
	REMOVE EXISTING CONCRETE WALL
	REMOVE EXISTING PAVEMENT MARKING
	FULL DEPTH SAWCUT
	REMOVE EXISTING UNDERGROUND COMM LINE, RE: TD101 & TD102
	REMOVE EXISTING UNDERGROUND ELECTRIC, RE: ED101 & ED102
	EXISTING UNDERGROUND MAIN FUEL PIPE TO REMAIN
	EXISTING PAVEMENT MARKING TO REMAIN
	TEMPORARY FENCE (FREE ZONE BOUNDARY), RE: A1/CS506

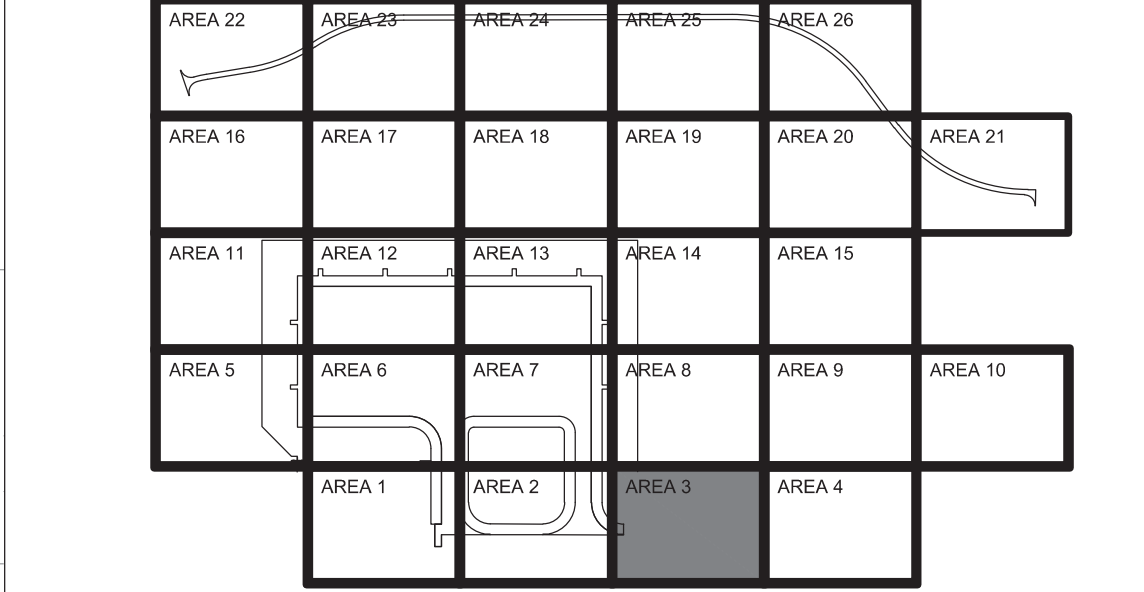


AREA 3 KEY PLAN	
GRAPHIC SCALE	
0 15' 30' 60'	
SCALE: 1"=30'	
NORTH ARROW	
TRUE N	

1	AMEND-002 - ADDED NOTE	10-MAR-26	DATE
1	DESCRIPTION		
JACOBS MEDONNELL JACOBS MEDONNELL A JOINT VENTURE 1100 NORTH GLEBE ROAD SUITE 500 ARLINGTON, VA 22201 A/E Contract No. 1665555-03-0003 A/E Task Order No. 1665555-03-0003 A/E Task Order No. 1665555-03-0003			
APPROVED Date: 3/10/2026 FOR COMMANDER NAVFAC DATE 04/10/2026			
ACTIVITY AFMISC APPROVAL PER NAVFAC SAT-TO CHECKLIST			
SATISFACTORY TO DATE 31 DEC 2025			
DES: JMH DRW: SMC REV: ATM			
PMIDM KKK			
BRANCH MANAGER SMK			
CHIEF ENGINEER SMK			
FIRE PROTECTION RO			
DEPARTMENT OF THE NAVY NAVAL FACILITIES ENGINEERING SYSTEMS COMMAND - PACIFIC NAVFAC PACIFIC ANDERSEN AIR FORCE BASE GUAM			
FY24 AUJY183012 (P-012), PDI: NORTH AIRCRAFT PARKING RAMP DEMOLITION PLAN - AREA 3			
SCALE: AS SHOWN EPROJETS NO.: 1665555 CONSTR CONTROL NO.			
NAVFAC DRAWING NO. 17361684			
SHEET 61 OF 377			
CD104			

REDESIGN FINAL SUBMITTAL


FILE NAME: U:\BLDG NAVFAC Pacific\03430603 - P-012 North Aircraft Parking Ramp\700 Working Documents\740 Sheets\740.01 Civil\012_1665555_CD107.dwg
LAYOUT NAME: DEMOLITION PLAN - AREA 6
PLOTED: 03/16/2026 7:07pm
USER: CameroS

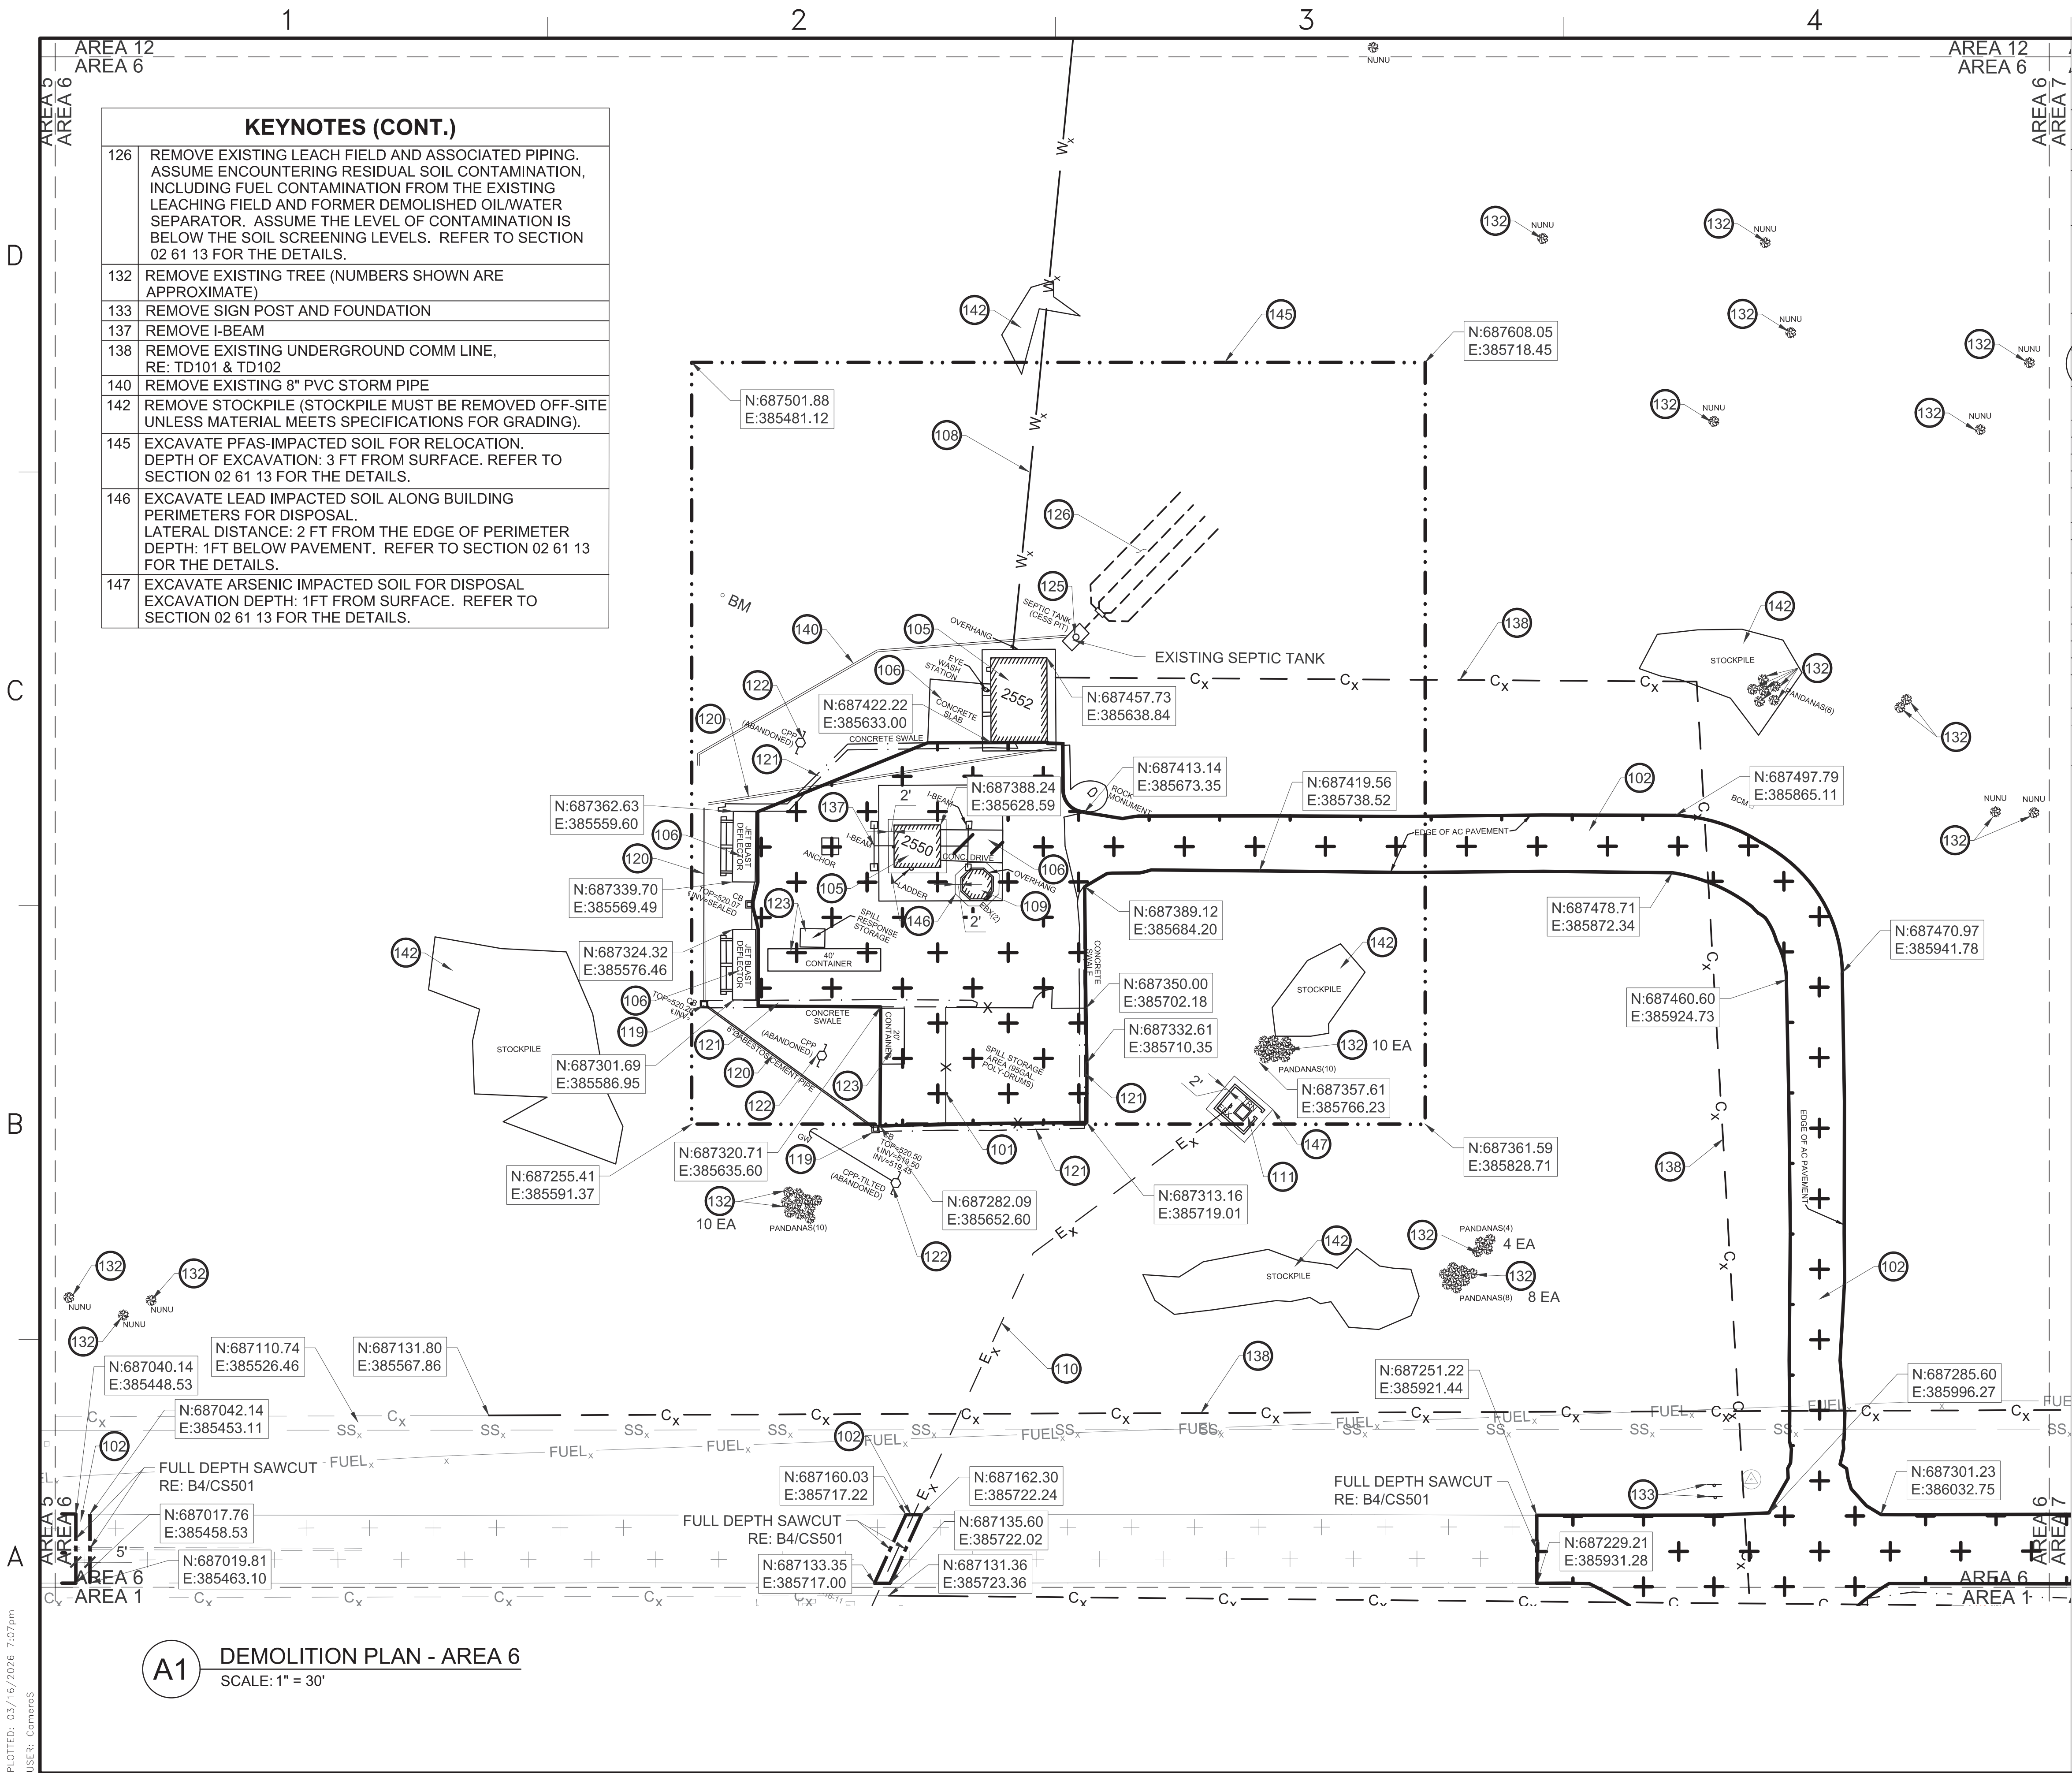

- ### GENERAL NOTES
- A EXISTING IMPROVEMENTS NOT SHOWN REMOVED ON DEMOLITION PLAN SHEETS MUST BE PROTECTED IN PLACE.
 - B CUT A STRAIGHT EDGE ALONG EXISTING ASPHALT PAVEMENT FOR INSTALLATION OF NEW PAVEMENT.
 - C PROTECT EXISTING EDGES OF PAVEMENT TO REMAIN.
 - D EXISTING SECURITY FENCE MUST REMAIN IN PLACE UNTIL TEMPORARY OR PERMANENT FENCING IS INSTALLED AND ACCEPTED. THE AIRFIELD MUST BE SECURE AT ALL TIMES.
 - E COMPLY WITH ENVIRONMENTAL REQUIREMENTS AND REGULATIONS. REFER TO DIVISIONS 01 AND 02 SPECIFICATIONS. REFER TO SECTIONS 02 82 00; 02 83 00; 02 84 16; AND 02 84 33 FOR LOCATIONS OF HAZARDOUS BUILDING MATERIALS AND PROJECT REQUIREMENTS.
 - F EXCAVATE PFAS, LEAD, OR ARSENIC-IMPACTED SOIL FOR RELOCATION. REFER TO CD115 RELOCATION AREA.
 - G FOR BIDDING PURPOSES, ASSUME THE THICKNESS OF THE EXISTING ASPHALT IS 6-INCHES.

- ### KEYNOTES
- 101 REMOVE EXISTING SECURITY FENCE
 - 102 REMOVE EXISTING ASPHALT PAVEMENT
 - 105 REMOVE EXISTING BUILDING AND FOUNDATION
 - 106 REMOVE EXISTING CONCRETE PAD
 - 108 REMOVE EXISTING WATERLINE (ASSUME ASBESTOS CEMENT PIPES)
 - 109 REMOVE EXISTING B2551
 - 110 REMOVE EXISTING UNDERGROUND ELECTRIC, RE: ED101 & ED102
 - 111 REMOVE EXISTING PAD-MOUNTED TRANSFORMER AND FOUNDATION, RE: ED101
 - 119 REMOVE EXISTING CATCH BASIN
 - 120 REMOVE EXISTING 6" ASBESTOS CEMENT STORM PIPE
 - 121 REMOVE EXISTING CONCRETE SWALE
 - 122 REMOVE EXISTING ABANDONED POWER POLE
 - 123 REMOVE EXISTING SPILL RESPONSE STORAGE AND 20' AND 40' CONTAINER
 - 125 REMOVE EXISTING SEPTIC TANK

- ### LEGEND
- REMOVE ASPHALT PAVEMENT
 - EXISTING ASPHALT PAVEMENT TO REMAIN
 - REMOVE EXISTING BUILDING
 - REMOVE EXISTING SITE FENCE
 - PFAS EXCAVATION AREA
 - FULL DEPTH SAWCUT
 - REMOVE EXISTING WATERLINE
 - REMOVE EXISTING UNDERGROUND ELECTRIC, RE: ED101 & ED102
 - REMOVE EXISTING UNDERGROUND COMM LINE, RE: TD101 & TD102
 - EXISTING SANITARY TO REMAIN
 - EXISTING UNDERGROUND MAIN FUEL PIPE TO REMAIN
 - EXISTING UNDERGROUND COMM. TO REMAIN
 - SURVEY CONTROL POINT
 - REMOVE EXISTING TREE
 - REMOVE EXISTING ABANDONED ELECTRICAL POLE
 - REMOVE EXISTING ROADWAY SIGN
 - REMOVE EXISTING CATCH BASIN

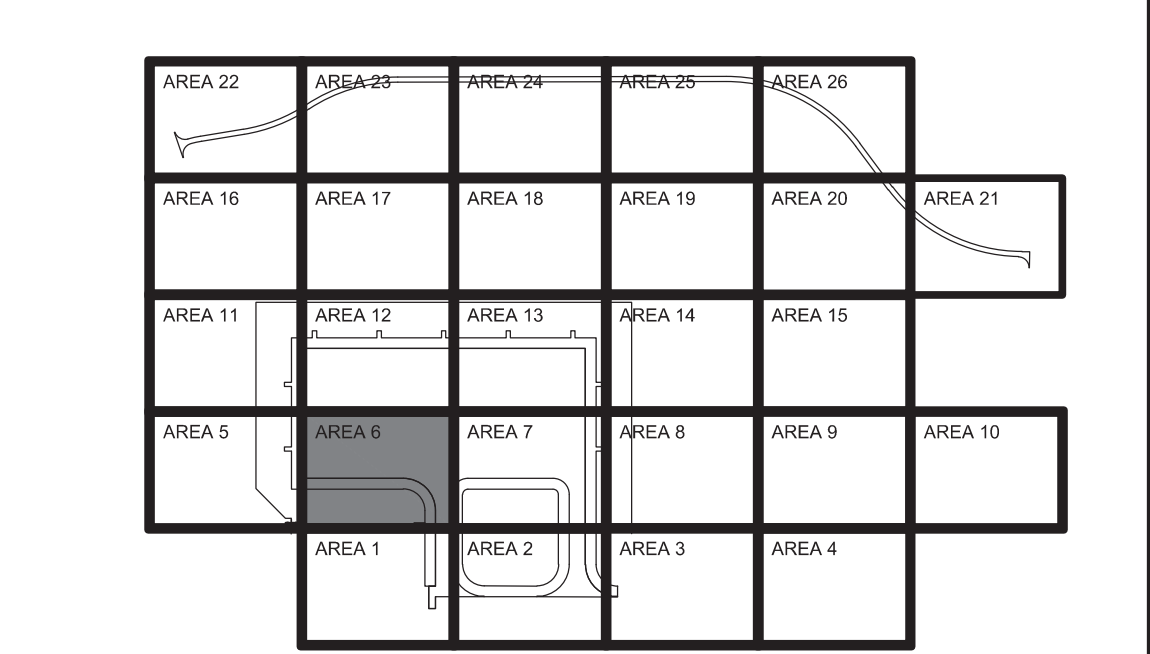

AREA 6 KEY PLAN

GRAPHIC SCALE

0 15' 30' 60'

SCALE: 1"=30'

NORTH ARROW

TRUE N

SCALE: AS SHOWN

PROJECTS NO.: 1665555

CONSTR CONTROL NO.

NAVFAC DRAWING NO. 17361687

SHEET 54 OF 377

CD107

REDESIGN FINAL SUBMITTAL

NAVFAC PACIFIC

ANDERSEN AIR FORCE BASE

NAVAFAC PACIFIC

NAVAL FACILITIES ENGINEERING SYSTEMS COMMAND - PACIFIC

JOINT REGION MARIANAS (JRM)

GUAM

FY24 AUJY183012 (P-012), PDI: NORTH AIRCRAFT PARKING RAMP - AREA 6

DEMOLITION PLAN - AREA 6

DATE: 04/MAR/26

SYMBOL DESCRIPTION

1. AMEND-002-ADDED NOTE

90167

JENNIFER M. HAYNES

PROFESSIONAL ENGINEER

3/10/2026

SEAL

JACOBS BURNS & MCDONNELL

JACOBSRAM A JOINT VENTURE

1100 NORTH GLEBE ROAD

SUITE 500

ARLINGTON, VA 22201

A/E/C CONTRACT NO. 1665555-0002

A/E Task Order No. 1665555-0002

A/E Task Order No. 1665555-0002

APPROVED

DATE: 04/10/2026

FOR COMMANDER NAVFAC

ACTIVITY

AFMISC APPROVAL PER NAVFAC

SAT-TO CHECKLIST

SATISFACTORY TO DATE

31 DEC 2026

DES: JMH DRW: SMC REV: ATM


PMIDM KKK

BRANCH MANAGER SMK

CHIEF ENGINEER SMK

FIRE PROTECTION RO


FILE NAME: U:\BLOG\NAVFAC Pacific\03430603 - P-012 North Aircraft Parking Ramp\700 Working Documents\740 Sheets\740.01 Civil\2012_1665555_CD109.dwg
LAYOUT NAME: DEMOLITION PLAN - AREA 8
PLOTED: 03/16/2026 7:12pm
USER: CameroS

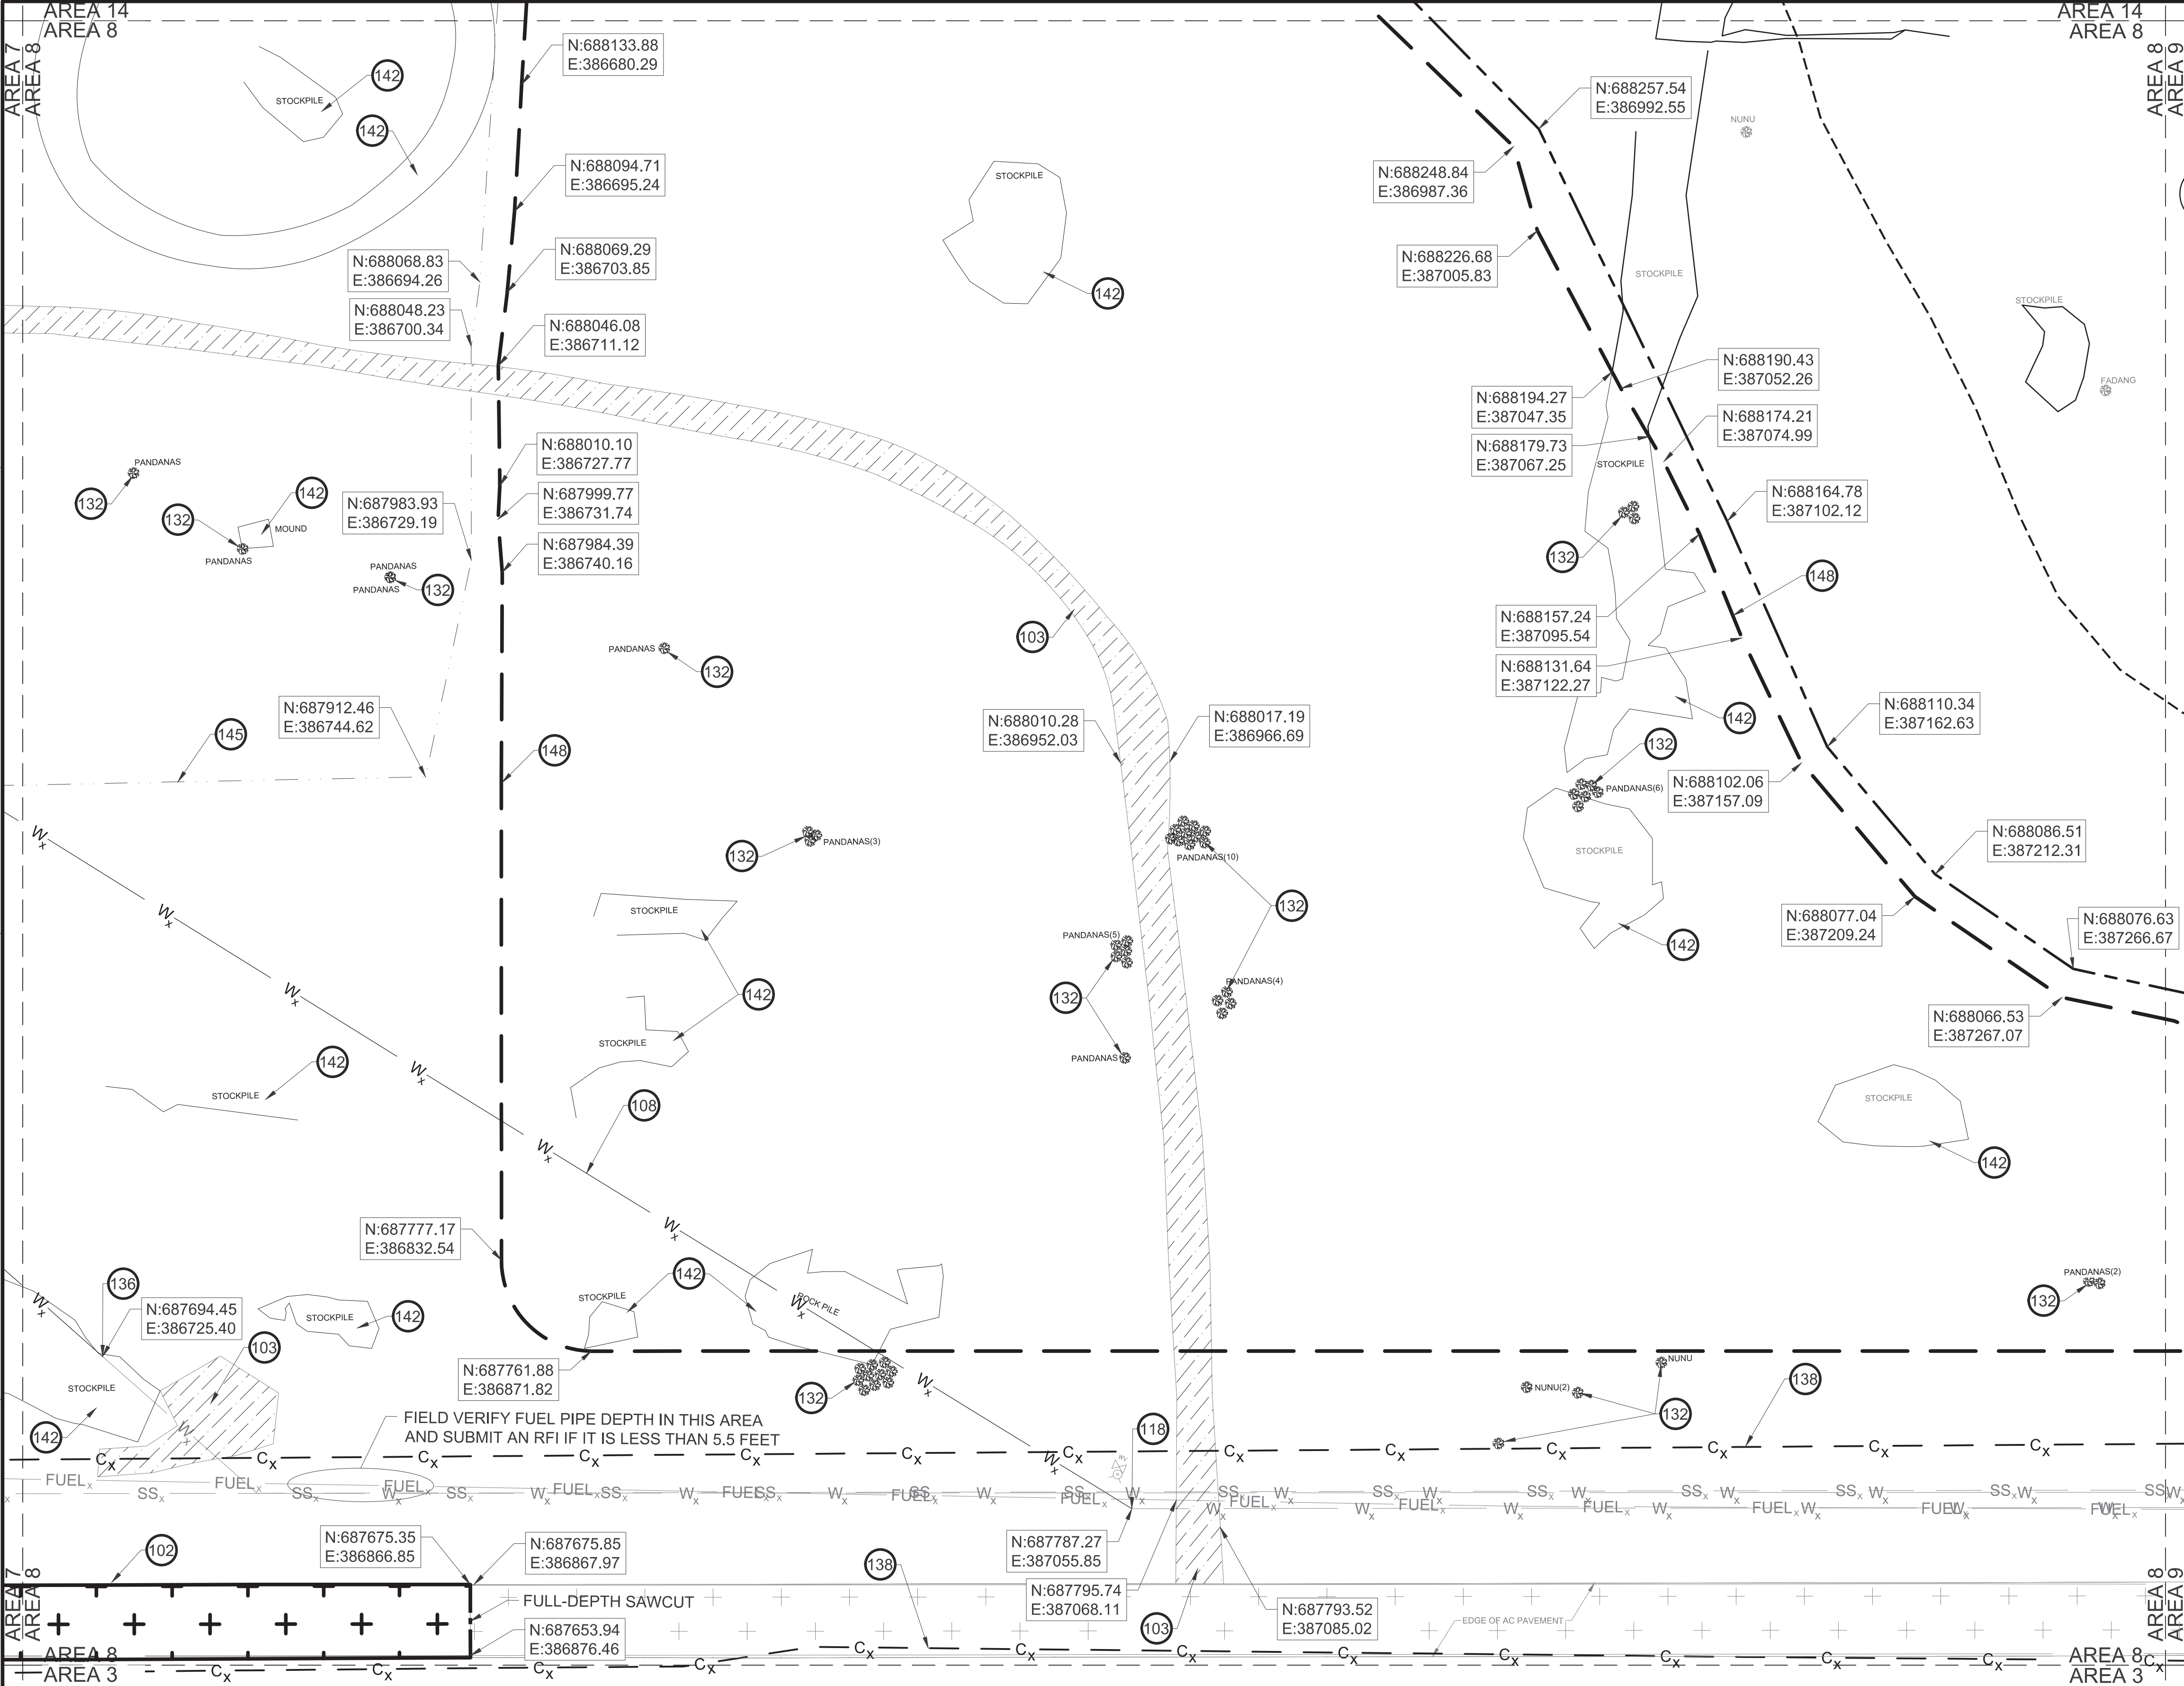

GENERAL NOTES	
A	EXISTING IMPROVEMENTS NOT SHOWN REMOVED ON DEMOLITION PLAN SHEETS MUST BE PROTECTED IN PLACE.
B	CUT A STRAIGHT EDGE ALONG EXISTING ASPHALT PAVEMENT FOR INSTALLATION OF NEW PAVEMENT.
C	COMPLY WITH ENVIRONMENTAL REQUIREMENTS AND REGULATIONS. REFER TO DIVISIONS 01 AND 02 SPECIFICATIONS.
D	FOR BIDDING PURPOSES, ASSUME THE THICKNESS OF THE EXISTING ASPHALT IS 6-INCHES.

KEYNOTES	
102	REMOVE EXISTING ASPHALT PAVEMENT
103	ABANDON EXISTING DIRT ROAD
108	REMOVE EXISTING WATERLINE (ASSUME ASBESTOS CEMENT PIPES)
118	CAP EXISTING WATERLINE
132	REMOVE EXISTING TREE (NUMBERS SHOWN ARE APPROXIMATE)
138	REMOVE EXISTING UNDERGROUND COMM LINE, RE: TD101 & TD102
142	REMOVE STOCKPILE (STOCKPILE MUST BE REMOVED OFF-SITE UNLESS MATERIAL MEETS SPECIFICATIONS FOR GRADING).
145	EXCAVATE PFAS-IMPACTED SOIL FOR RELOCATION. DEPTH OF EXCAVATION: 3 FT FROM SURFACE. REFER TO SECTION 02 61 13 FOR THE DETAILS.
148	RELOCATE PFAS-IMPACTED SOIL. PROVIDE GEOMEMBRANE BARRIER TO WRAP RELOCATED IMPACTED SOIL. PROVIDE A MINIMUM 1-FOOT LAYER OF VEGETATED CLEAN SOIL CAP. REFER TO SECTION 02 61 13 FOR THE DETAILS.

LEGEND	
	REMOVE ASPHALT PAVEMENT
	REMOVE DIRT ROAD
	EXISTING ASPHALT PAVEMENT TO REMAIN
	REMOVE EXISTING WATERLINE
	REMOVE EXISTING UNDERGROUND COMM LINE, RE: TD101 & TD102
	EXISTING SINKHOLE
	LIMITS OF DISTURBANCE
	PFAS EXCAVATION AREA
	PFAS RELOCATION AREA
	FULL DEPTH SAWCUT
	EXISTING WATERLINE TO REMAIN
	EXISTING UNDERGROUND FUEL LINE TO REMAIN
	EXISTING SANITARY TO REMAIN
	EXISTING UNDERGROUND COMM. TO REMAIN
	EXISTING FIRE HYDRANT TO REMAIN
	EXISTING WATER VALVE TO REMAIN
	REMOVE EXISTING TREE
	EXISTING TREE TO REMAIN

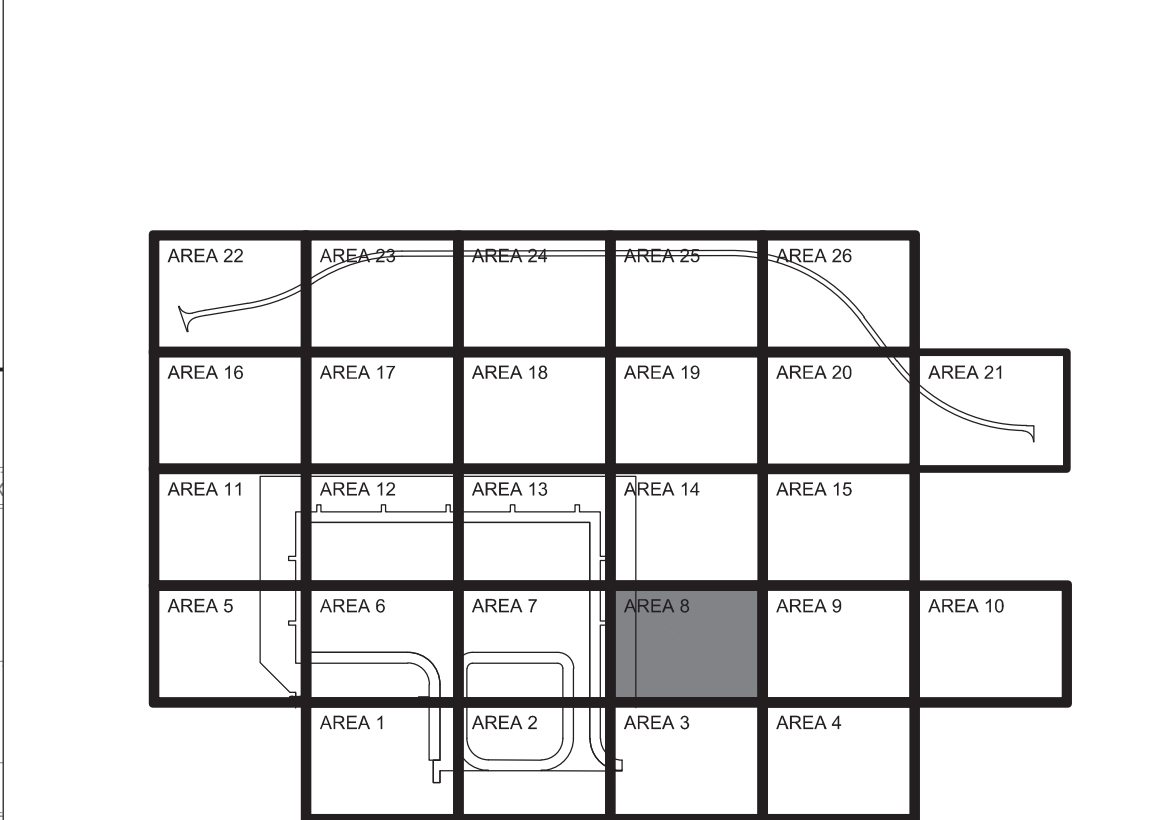

AREA 8 KEY PLAN	
GRAPHIC SCALE	
0 15' 30' 60'	
SCALE: 1"=30'	
NORTH ARROW	
TRUE N	

1	AMEND-002-ADDED NOTE	13-MAR-26	DATE
1	SYNOPSIS		

NAVFAC

JACOBS BURNS & MCDONNELL

JACOBS BURN A JOINT VENTURE
1100 NORTH GLEBE ROAD
SUITE 500
ARLINGTON, VA 22201

ALL OTHERS: N/A
ALL OTHERS: N/A
ALL OTHERS: N/A

APPROVED

FOR COMMANDER NAVFAC DATE 04/10/2026

ACTIVITY

AFMISC APPROVAL PER NAVFAC SAT-TO CHECKLIST

SATISFACTORY TO DATE 31 DEC 2025

DES: JMH DRW: SMC REV: ATM

PMIDM KKK

BRANCH MANAGER SMK

CHIEF ENGINEER SMK

FIRE PROTECTION RO

DEPARTMENT OF THE NAVY

NAVAL FACILITIES ENGINEERING SYSTEMS COMMAND

NAVAL FACILITIES ENGINEERING SYSTEMS COMMAND - PACIFIC

NAVFAC PACIFIC

ANDERSEN AIR FORCE BASE

GUAM

FY24 AUJY183012 (P-012),
PDI: NORTH AIRCRAFT PARKING RAMP
DEMOLITION PLAN - AREA 8

SCALE: AS SHOWN


EPROJETS NO.: 1665555

CONSTR CONTROL NO.

NAVFAC DRAWING NO. 17361689

SHEET 85 OF 377




CD109


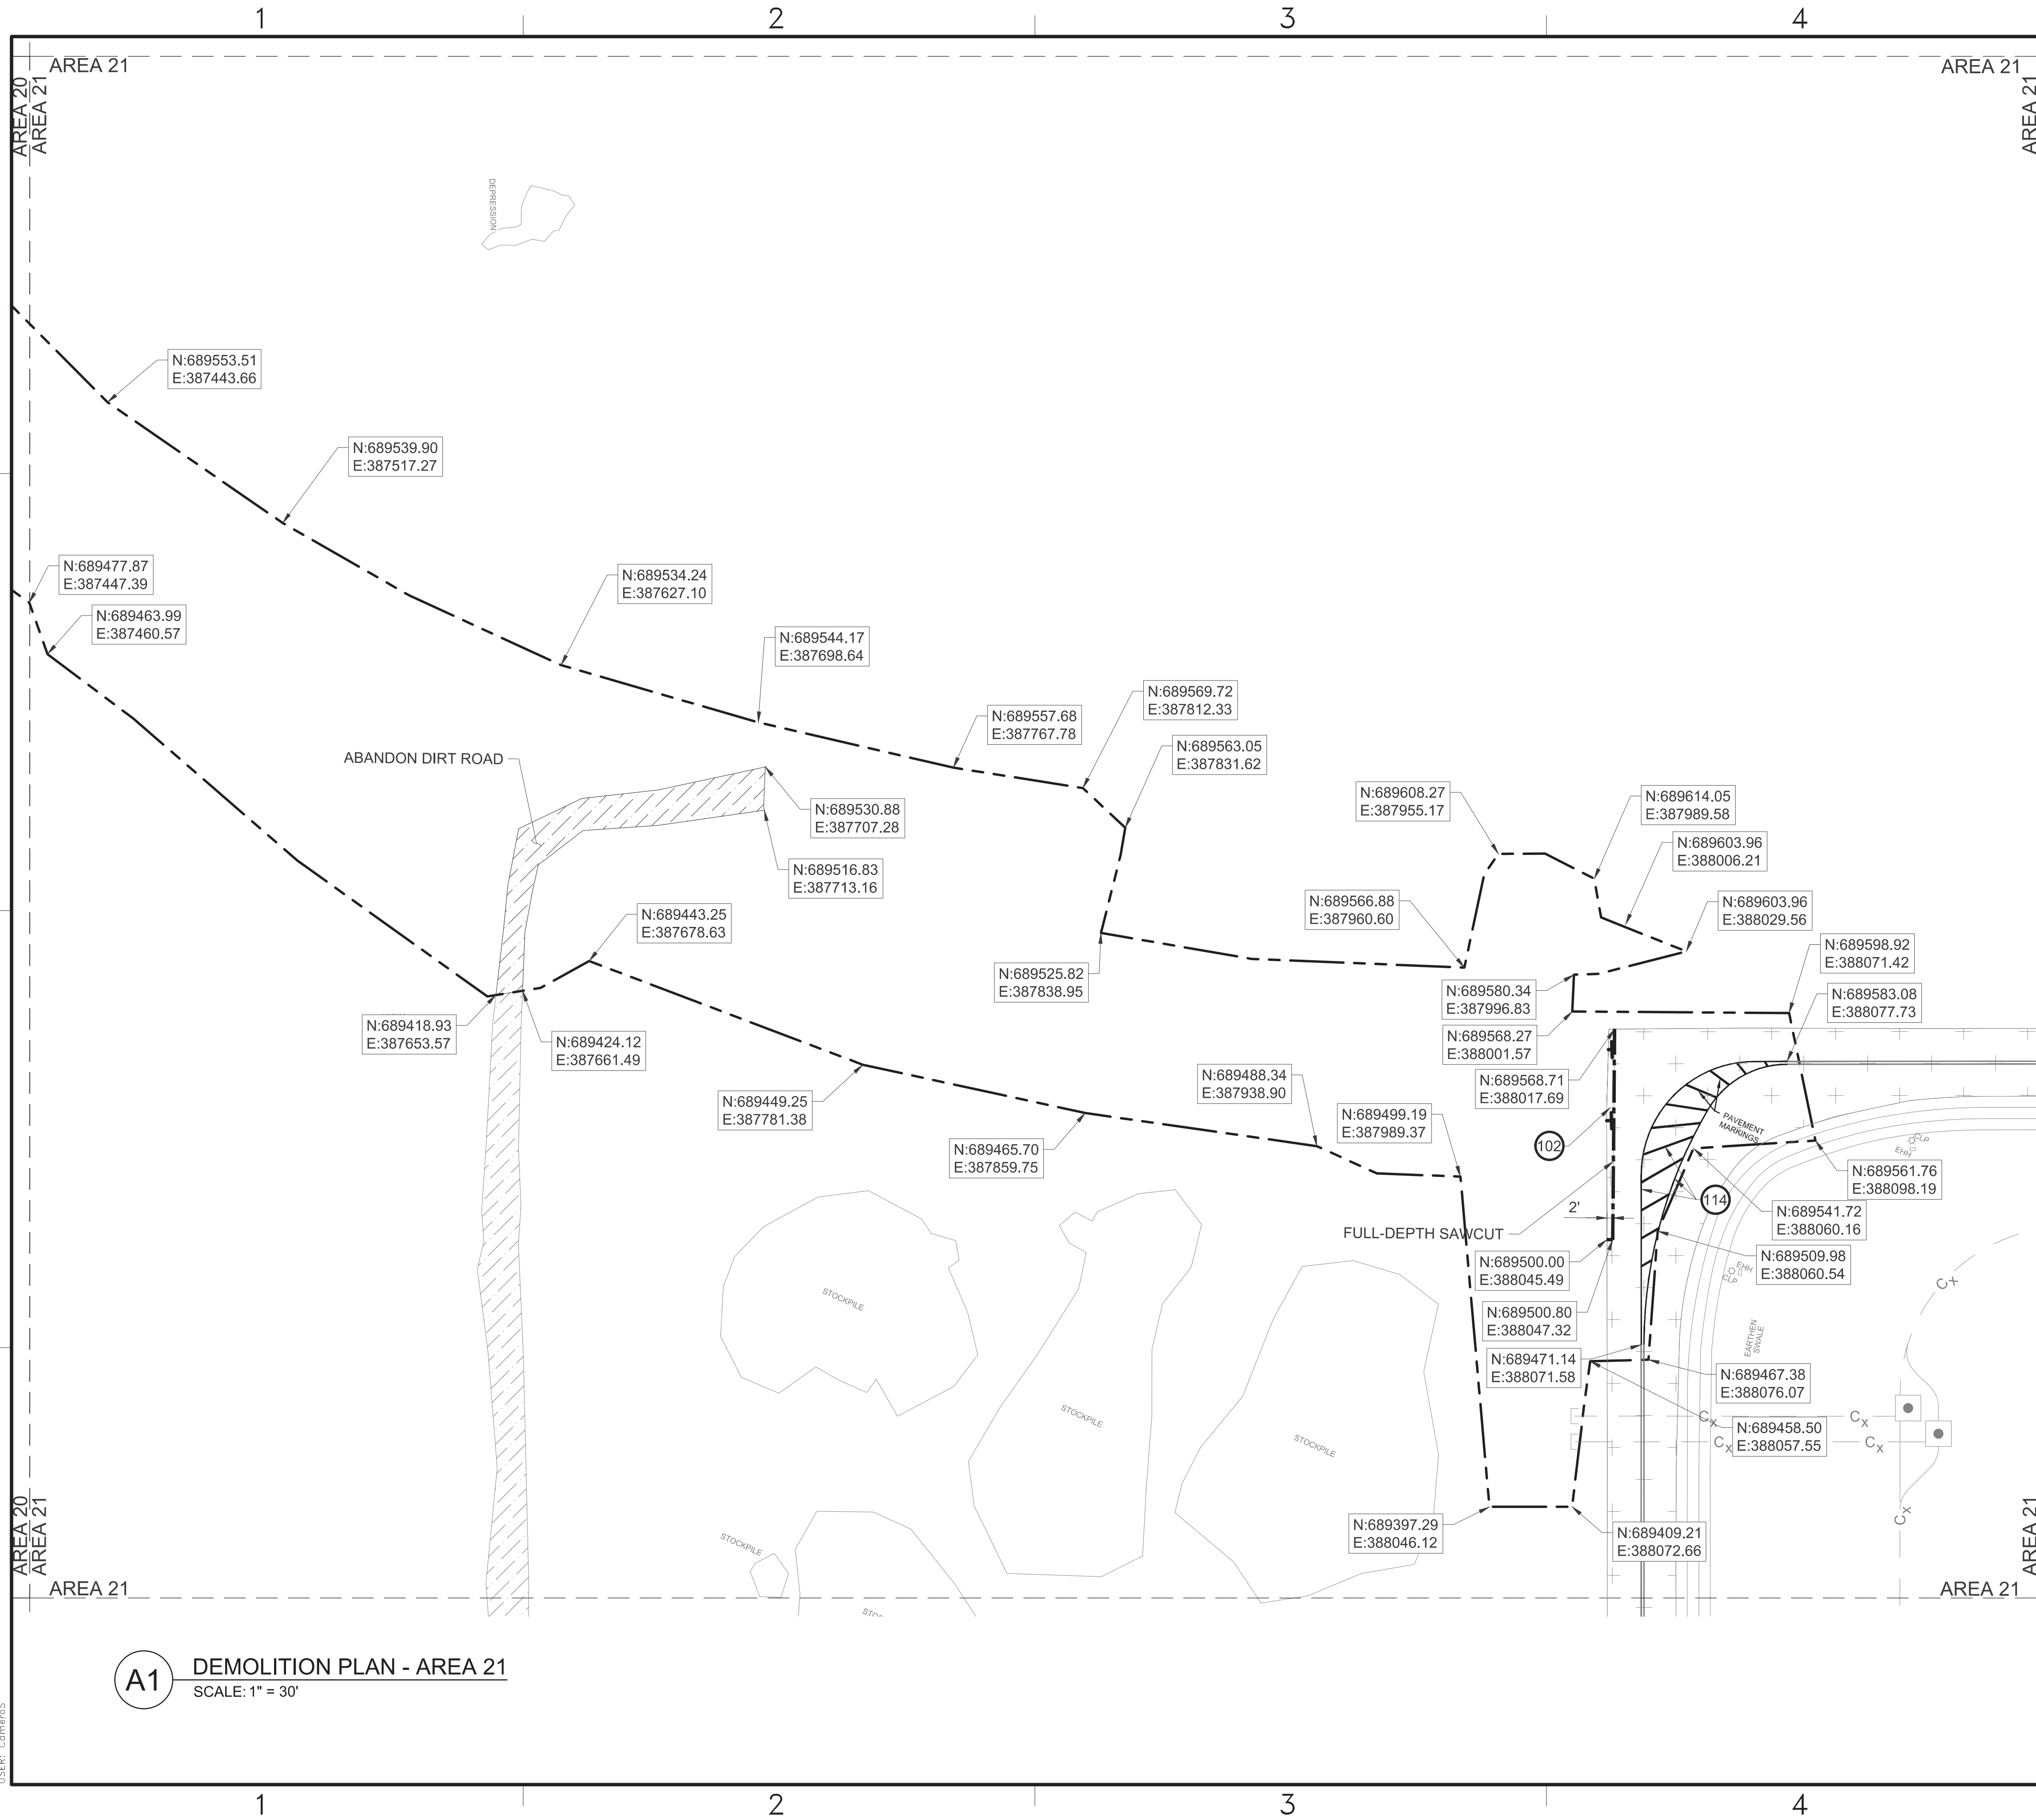


GENERAL NOTES	
A	EXISTING IMPROVEMENTS NOT SHOWN REMOVED ON DEMOLITION PLAN SHEETS MUST BE PROTECTED IN PLACE.
B	CUT A STRAIGHT EDGE ALONG EXISTING ASPHALT PAVEMENT FOR INSTALLATION OF NEW PAVEMENT.
C	PROTECT EXISTING EDGES OF PAVEMENT TO REMAIN.
D	COMPLY WITH ENVIRONMENTAL REQUIREMENTS AND REGULATIONS. REFER TO DIVISIONS 01 AND 02 SPECIFICATIONS.
E	FOR BIDDING PURPOSES, ASSUME THE THICKNESS OF THE EXISTING ASPHALT IS 6-INCHES.


KEYNOTES	
102	REMOVE EXISTING ASPHALT PAVEMENT
114	REMOVE EXISTING PAVEMENT MARKING

LEGEND

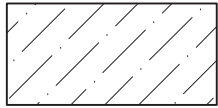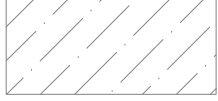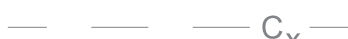	REMOVE ASPHALT PAVEMENT
	EXISTING ASPHALT PAVEMENT TO REMAIN
	REMOVE GRAVEL/DIRT ROAD
	EXISTING DIRT ROAD
	LIMITS OF DISTURBANCE
	FULL DEPTH SAWCUT
	EXISTING UNDERGROUND COMM. TO REMAIN
	EXISTING COMMUNICATION JUNCTION BOX TO REMAIN
	EXISTING LIGHT TO REMAIN

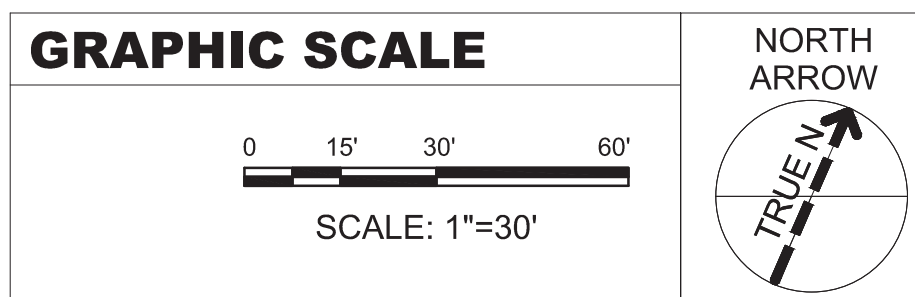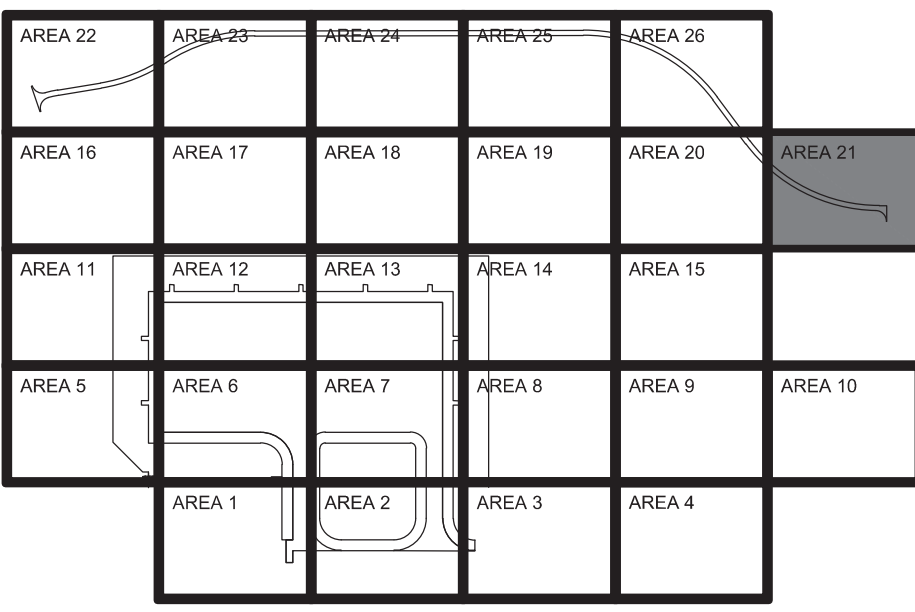[illegible]


FILE NAME: U:\BLDG NAVFAC Pacific\03430603 - P-012 North Aircraft Parking Ramp\700 Working Documents\740.01 Civil\012_1665555_CD123.dwg
LAYOUT NAME: DEMOLITION PLAN - AREA 22
PLOTED: 03/16/2026 7:19pm
USER: CameroS

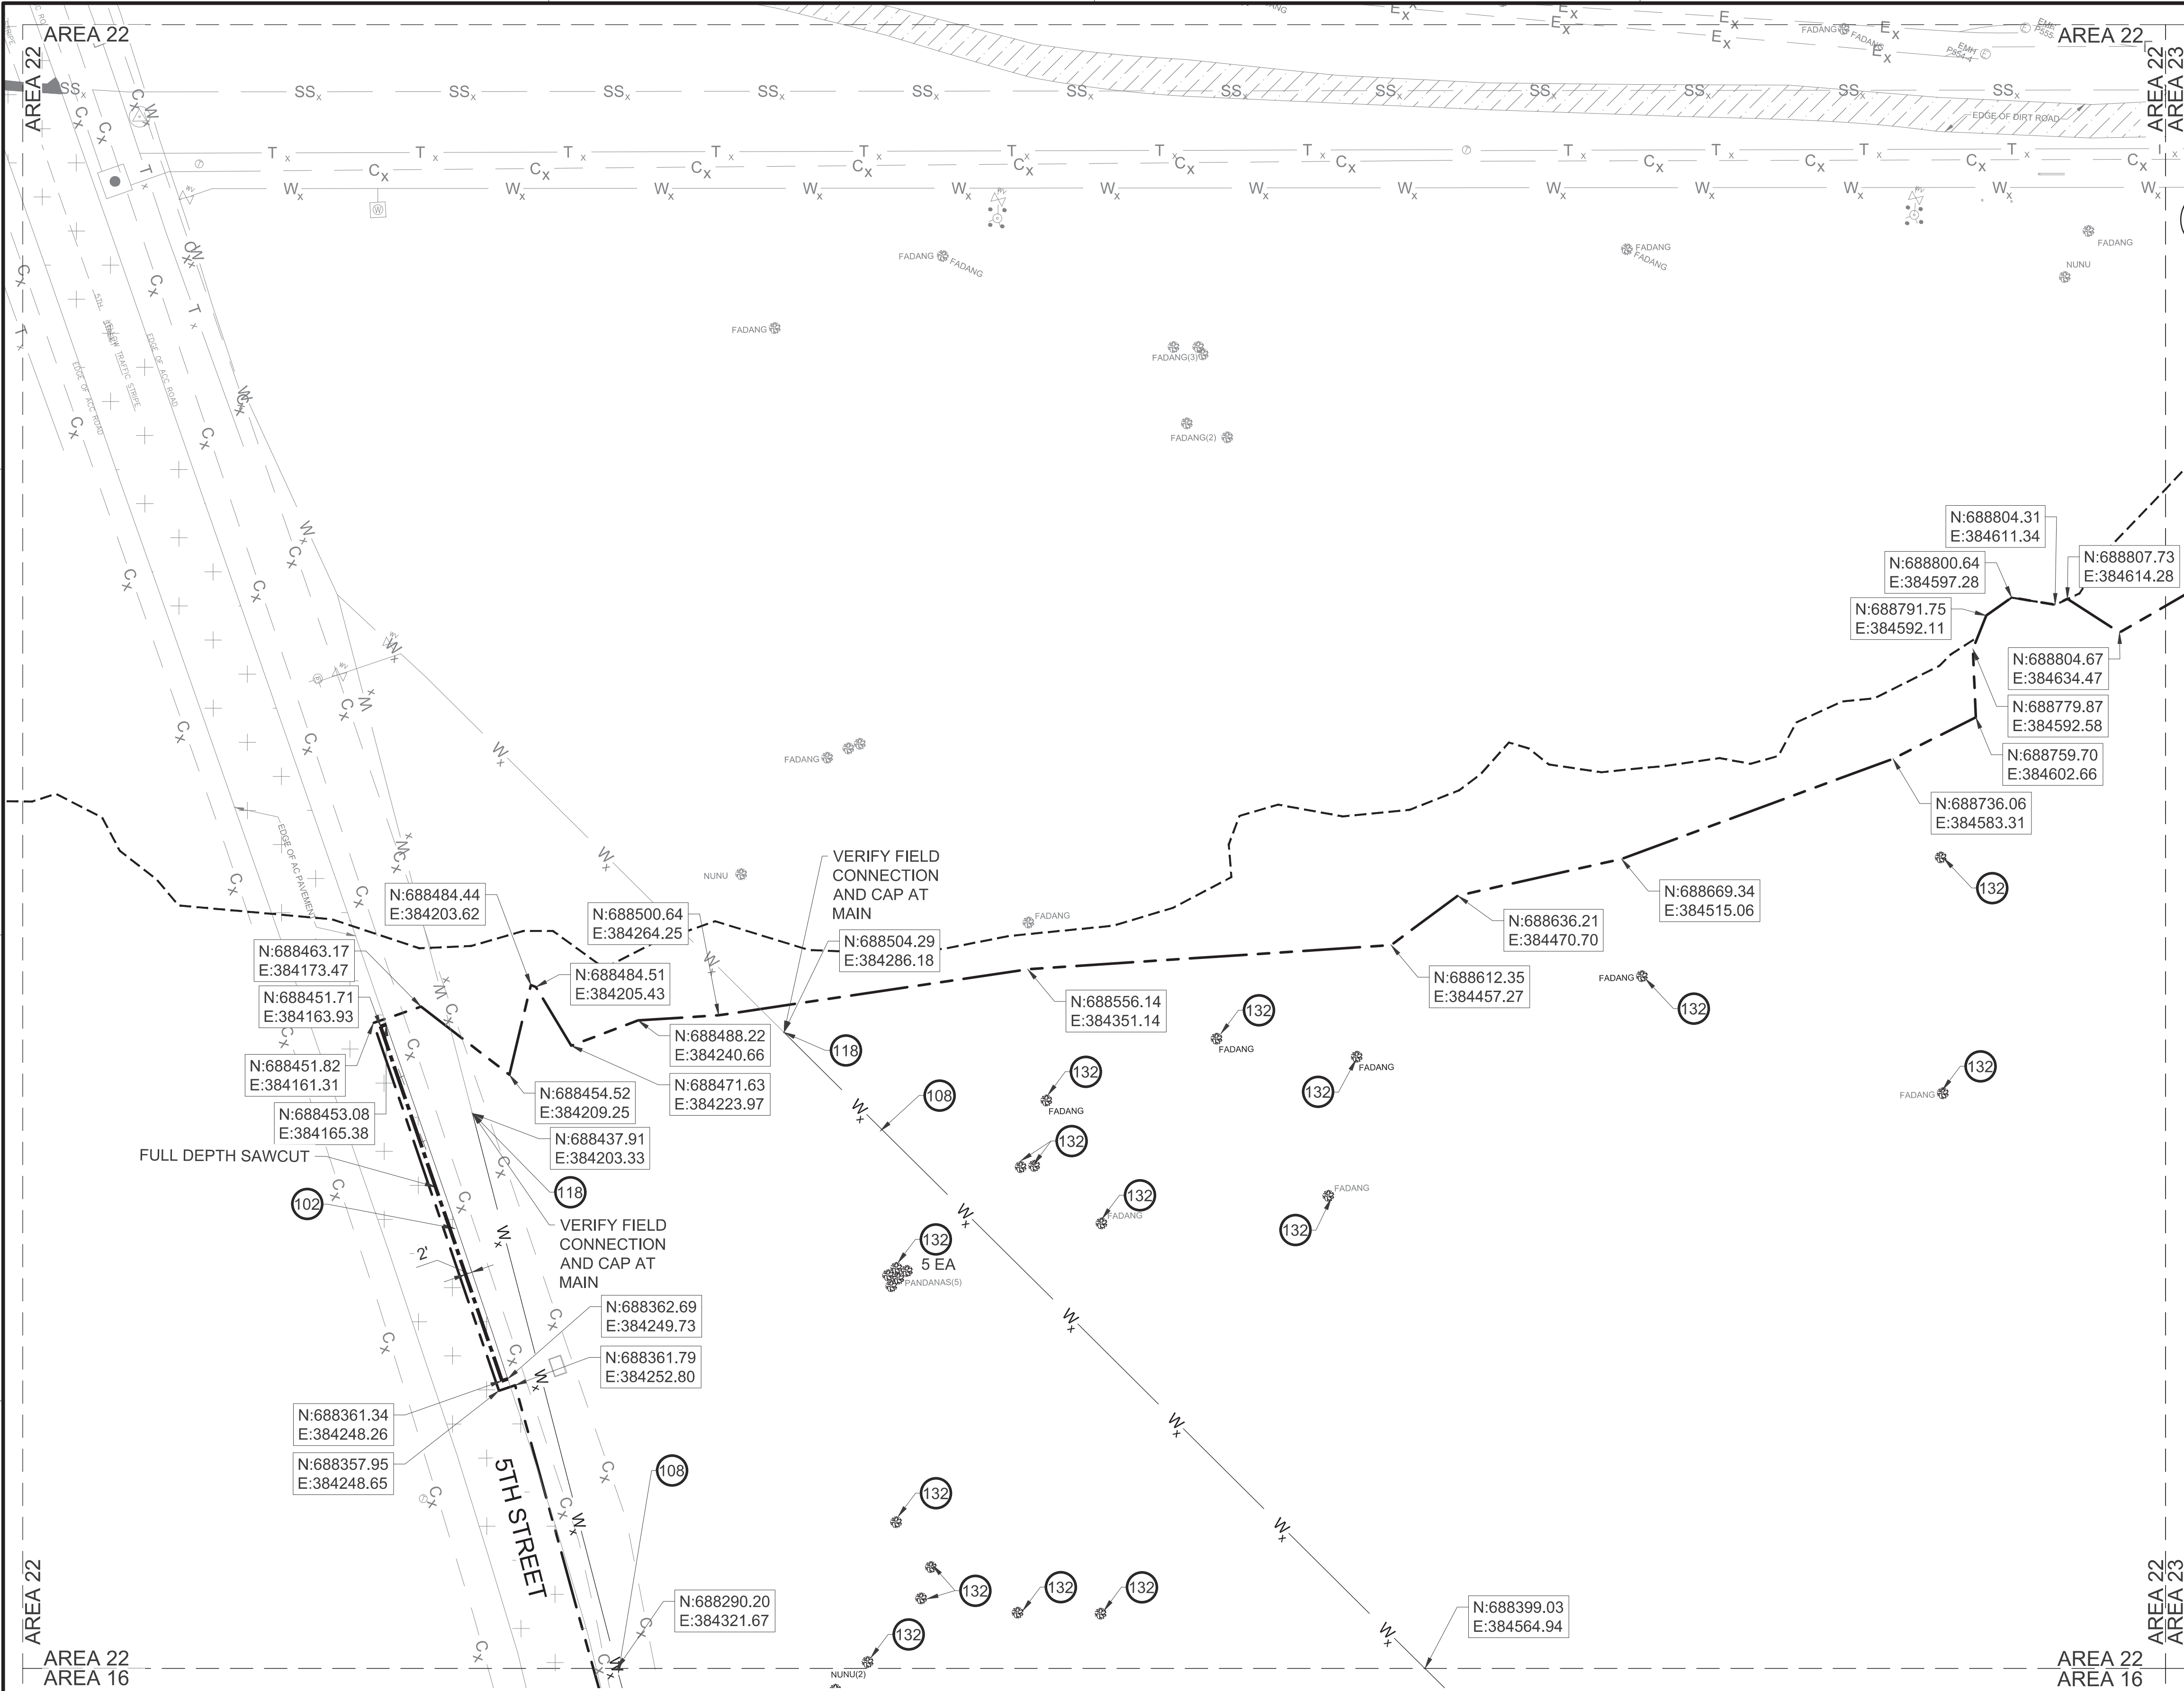

GENERAL NOTES	
A	EXISTING IMPROVEMENTS NOT SHOWN REMOVED ON DEMOLITION PLAN SHEETS MUST BE PROTECTED IN PLACE.
B	CUT A STRAIGHT EDGE ALONG EXISTING ASPHALT PAVEMENT FOR INSTALLATION OF NEW PAVEMENT.
C	PROTECT EXISTING EDGES OF PAVEMENT TO REMAIN.
D	COMPLY WITH ENVIRONMENTAL REQUIREMENTS AND REGULATIONS. REFER TO DIVISIONS 01 AND 02 SPECIFICATIONS.
E	FOR BIDDING PURPOSES, ASSUME THE THICKNESS OF THE EXISTING ASPHALT IS 6-INCHES.

KEYNOTES	
102	REMOVE EXISTING ASPHALT PAVEMENT
108	REMOVE EXISTING WATERLINE (ASSUME ASBESTOS CEMENT PIPES)
118	CAP EXISTING WATERLINE
132	REMOVE EXISTING TREE (NUMBERS SHOWN ARE APPROXIMATE)

LEGEND	
	REMOVE ASPHALT PAVEMENT
	EXISTING ASPHALT PAVEMENT TO REMAIN
	EXISTING DIRT ROAD
	LIMITS OF DISTURBANCE
	FULL DEPTH SAWCUT
	REMOVE EXISTING WATERLINE
	EXISTING UNDERGROUND COMM. TO REMAIN
	EXISTING WATERLINE TO REMAIN
	EXISTING SANITARY SEWER LINE TO REMAIN
	EXISTING UNDERGROUND ELECTRICAL LINE TO REMAIN
	EXISTING PHONE LINE TO REMAIN
	EXISTING SINKHOLE
	REMOVE EXISTING TREE
	EXISTING TREE TO REMAIN
	EXISTING COMMUNICATION MANHOLE/HANDHOLE TO REMAIN
	EXISTING WATER VALVE TO REMAIN
	EXISTING FIRE HYDRANT TO REMAIN
	EXISTING WATER METER TO REMAIN
	EXISTING COMMUNICATION JUNCTION BOX TO REMAIN
	EXISTING ELECTRICAL MANHOLE/HANDHOLE TO REMAIN
	SURVEY CONTROL POINT

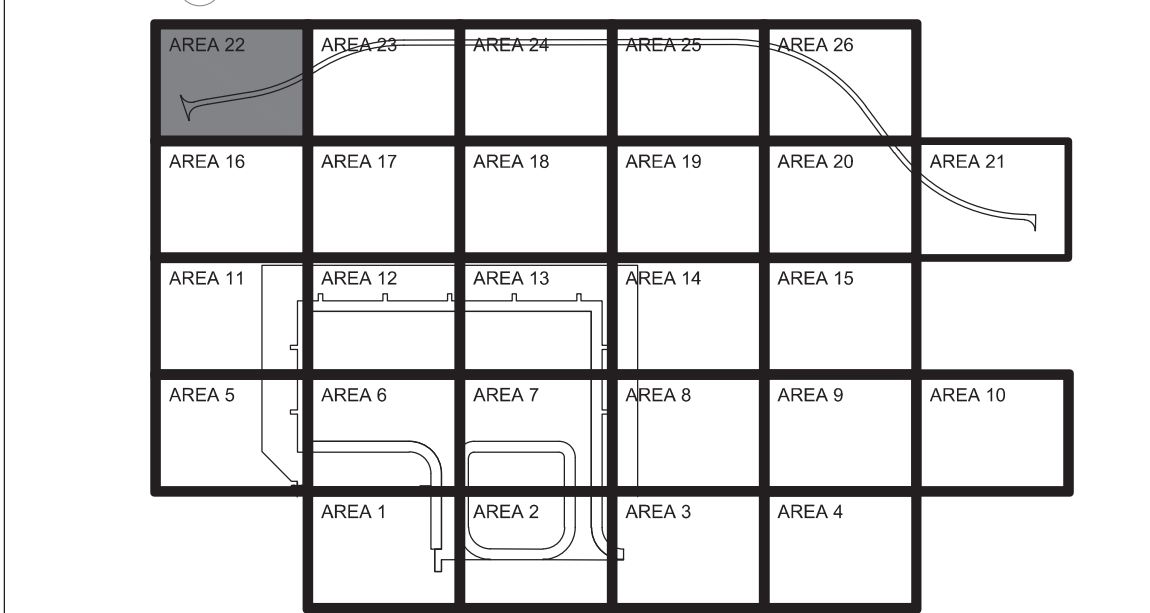


GRAPHIC SCALE	
	SCALE: 1"=30'
NORTH ARROW	

STATE OF TEXAS JENNIFER M. HAYNES 90167 LICENSED PROFESSIONAL ENGINEER 3/10/2026 SEAL	
Jacobs BURNS & MCDONNELL JACOBSRAM, A JOINT VENTURE 1100 NORTH GLEBE ROAD SUITE 500 ARLINGTON, VA 22201 A/E: 03/16/2026 A/E Task Order No. 1665555-0002 A/E Task Order No. 1665555-0003 A/E Task Order No. 1665555-0004 A/E Task Order No. 1665555-0005	
APPROVED DATE: 04/10/2026 FOR COMMANDER NAVFAC	
ACTIVITY AFMISC APPROVAL PER NAVFAC SAT-TO CHECKLIST	
SATISFACTORY TO DATE: 31 DEC 2026	
DES: JMH	DRW: SMC
REV: ATM	PMID: KKK
BRANCH MANAGER: SMK	CHIEF ENGINEER: SMK
FIRE PROTECTION: RO	
NAVAL FACILITIES ENGINEERING SYSTEMS COMMAND NAVAL FACILITIES ENGINEERING SYSTEMS COMMAND - PACIFIC JOINT REGION WARRIORS (JRW) GUAM FY24 AJJY183012 (P-012), PDI: NORTH AIRCRAFT PARKING RAMP DEMOLITION PLAN - AREA 22	
SCALE: AS SHOWN EPROJECTS NO.: 1665555 CONSTR CONTROL NO. NAVFAC DRAWING NO. 17361701 SHEET 79 OF 377	
CD123	

REDESIGN FINAL SUBMITTAL


FILE NAME: U:\BLDG NAVFAC Pacific\03430603 - P-012 North Aircraft Parking Ramp\700 Working Documents\740.01 Civil\012_1665555_CS123.dwg
LAYOUT NAME: SITE & PAVING PLAN - AREA 23
PLOTTED: 03/09/2026 12:01pm
USER: CameroS

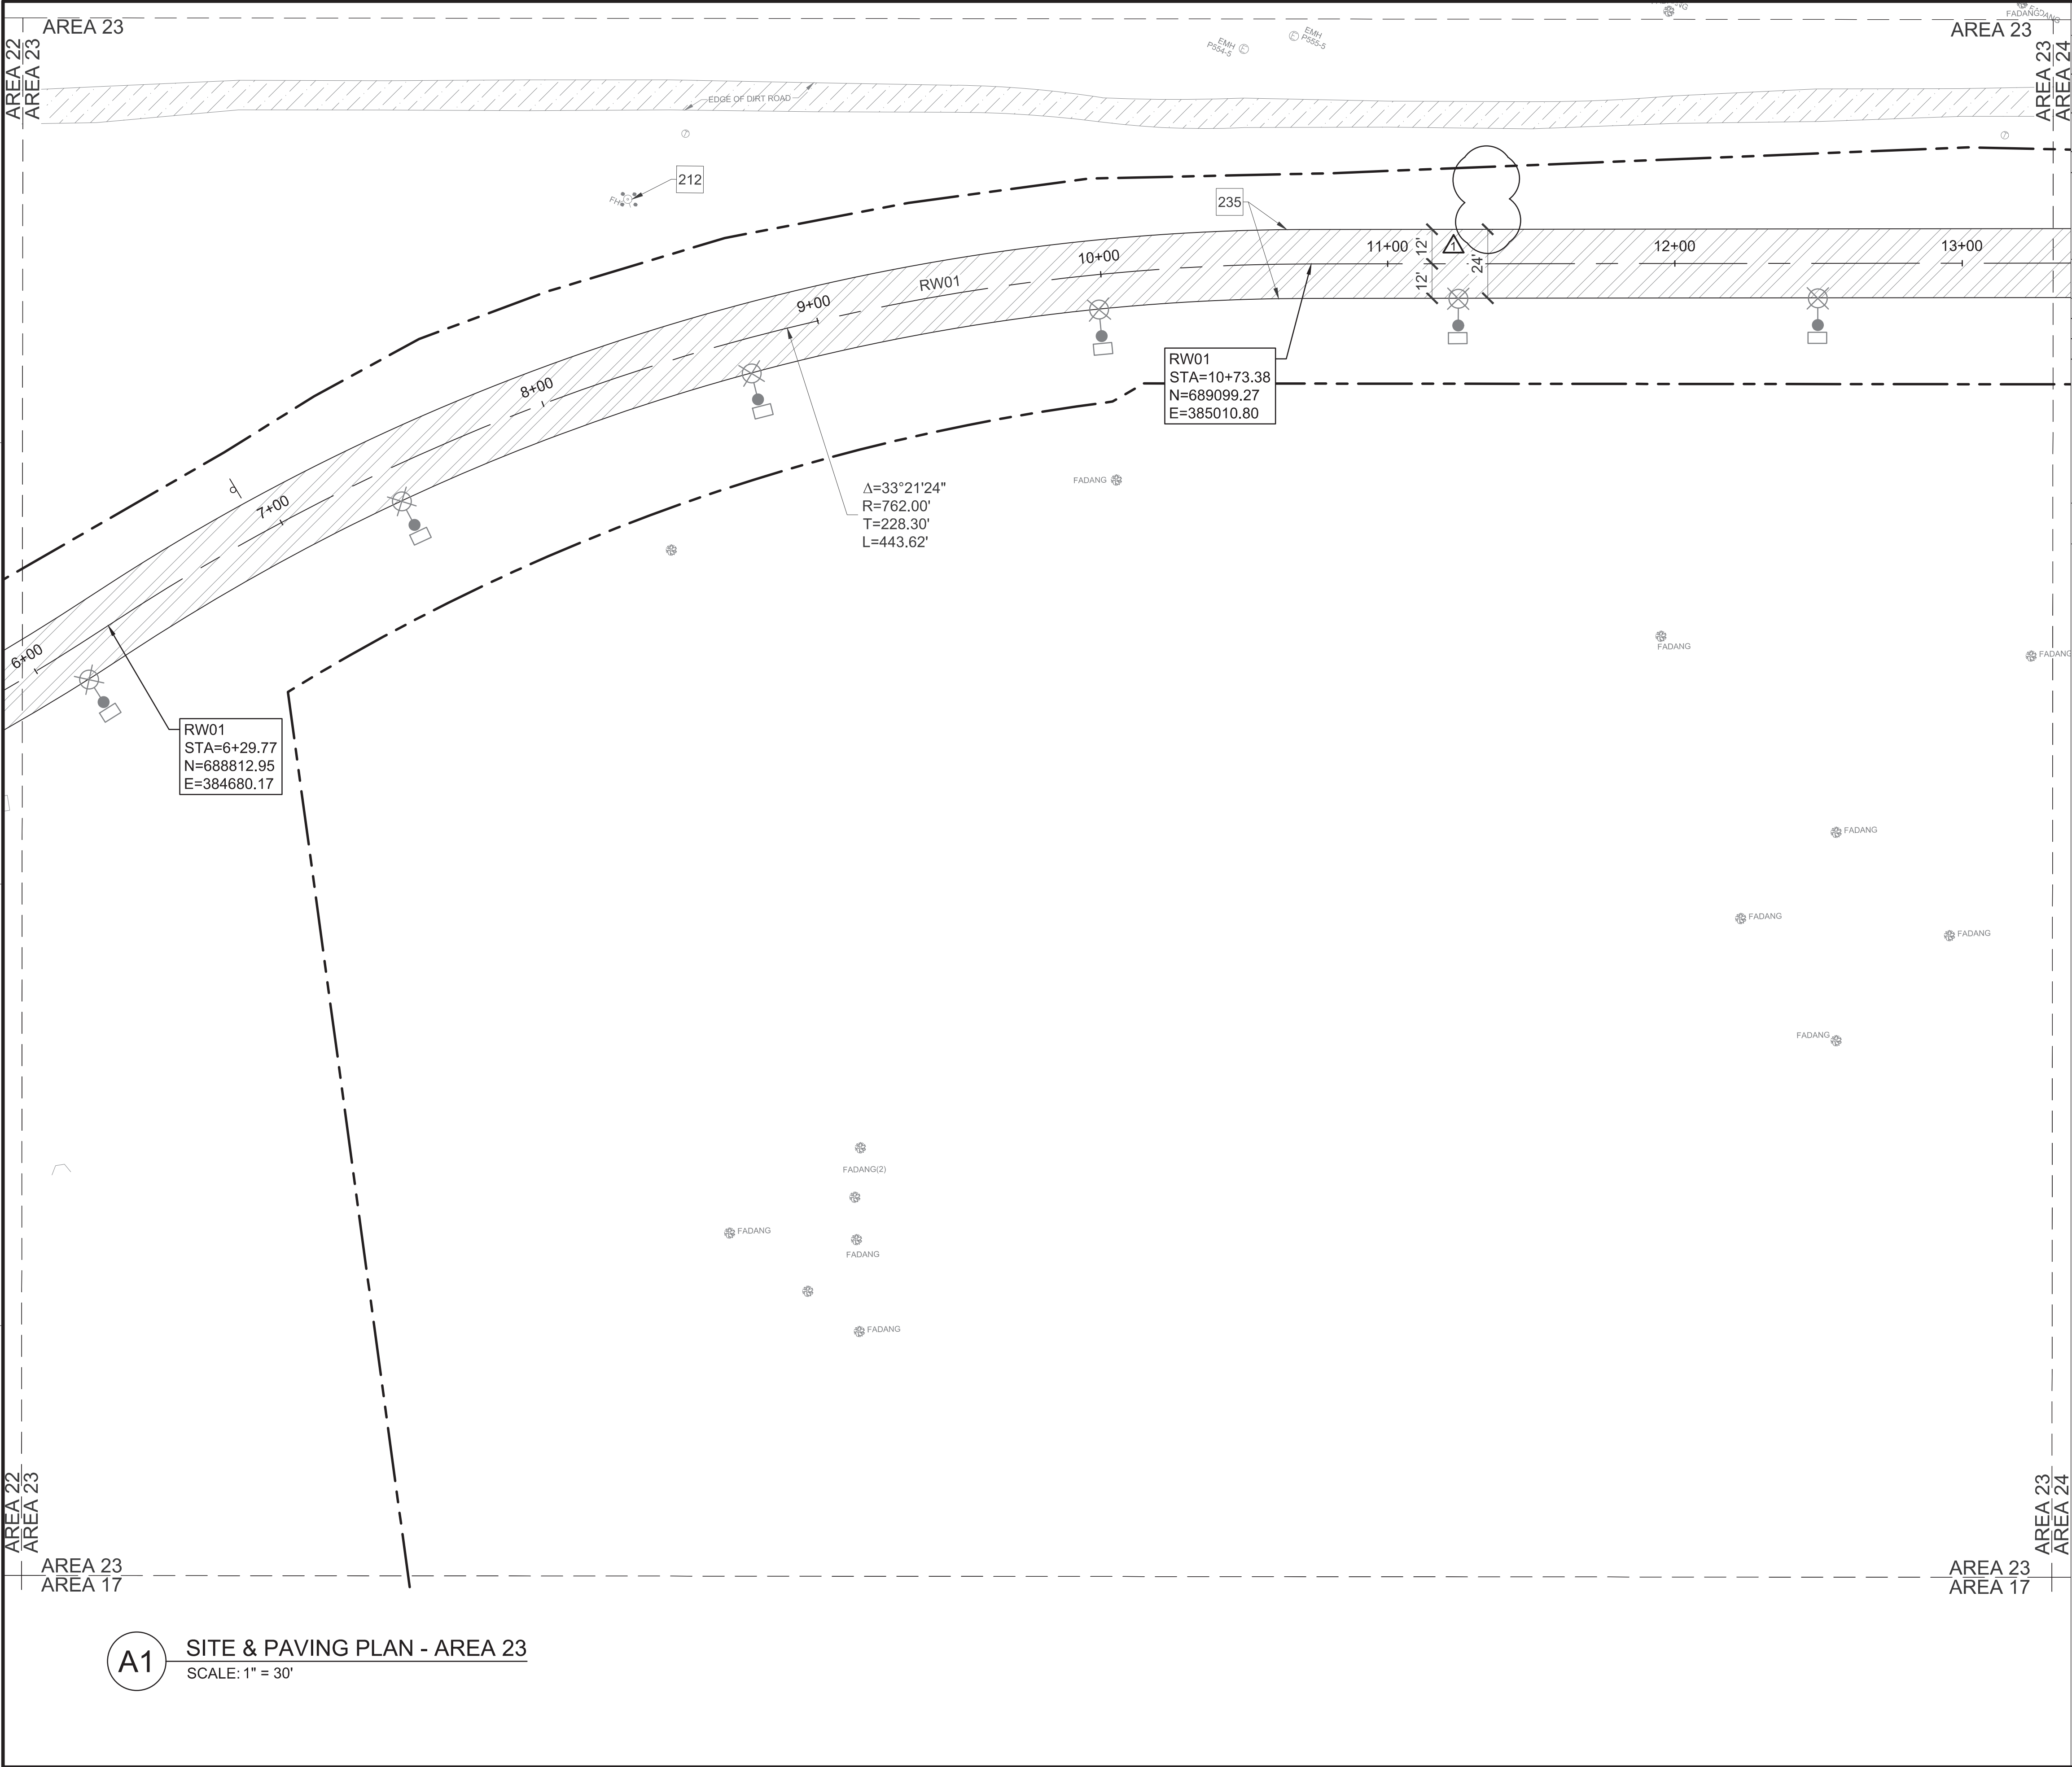

GENERAL NOTES	
A	DIMENSIONS ARE TO BACK OF CURB OR EDGE OF PAVEMENT, UNLESS NOTED OTHERWISE
B	REFER TO ELECTRICAL PLANS FOR SITE LIGHTING INFORMATION
C	REFER TO SHEETS CS130 - CS146 FOR PAVEMENT MARKING PLANS
D	REFER TO SHEETS CS201 - CS211 FOR ROADWAY PROFILES

KEYNOTES	
212	EXISTING FIRE HYDRANT
248	SPEED LIMIT SIGN (35 MPH), RE: A1/CS503
235	EDGE OF PAVEMENT / ASPHALT TAPER, RE: D4/CS501

LEGEND	
	ASPHALT ROADWAY, RE: C3/CS501
	EXISTING DIRT ROAD
	ROADWAY CENTERLINE
	LIMITS OF DISTURBANCE
	STREET LIGHT POLE, RE: A3/ES503
	EXISTING FIRE HYDRANT
	EXISTING COMMUNICATION MANHOLE
	EXISTING ELECTRICAL MANHOLE
	ELECTRICAL PULL BOX
	EXISTING TREE
	SPEED LIMIT SIGN (35 MPH), RE: A1/CS503

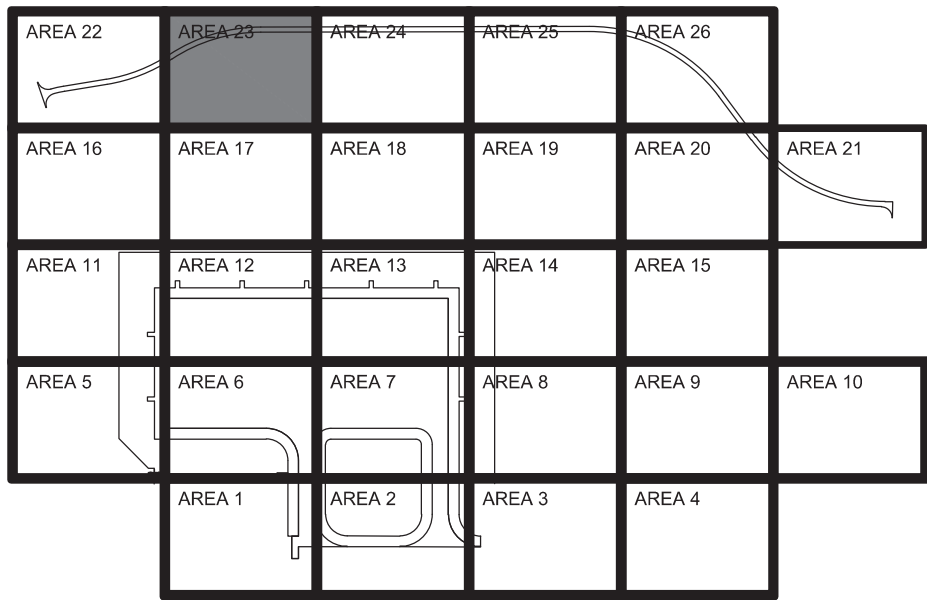

AREA 23
KEY PLAN

GRAPHIC SCALE

0 15' 30' 60'

SCALE: 1"=30'

NORTH
ARROW

TRUE N

10-MAR-26

DATE

1

AMEND.002 - REVISED FHS

SYM

DESCRIPTION

JACOBS

BURNS

MCDONNELL

JACOBSRAM, A JOINT VENTURE

1100 NORTH GLEBE ROAD

SUITE 500

ARLINGTON, VA 22201

A/E Contract No. N62172-24-2-0003

A/E Task Order No. N62172-24-2-0003

A/E Task Order No. N62172-24-2-0003

A/E Task Order No. N62172-24-2-0003

APPROVED

DATE 04/10/2026

FOR COMMANDER NAVFAC

DATE 04/10/2026

ACTIVITY

AFMISC APPROVAL PER NAVFAC

SAT-TO CHECKLIST

SATISFACTORY TO DATE

31 DEC 2025

DES: JMH

DRW: SMC

REV: ATM

PM/DM

KKK

BRANCH MANAGER

SMK

CHIEF ENGINEER

SMK

FIRE PROTECTION

RO

DEPARTMENT OF THE NAVY

NAVAL FACILITIES ENGINEERING SYSTEMS COMMAND

NAVAL FACILITIES ENGINEERING SYSTEMS COMMAND - PACIFIC

JOINT REGION MARIANAS (JRM)

NAVFAC PACIFIC

ANDERSEN AIR FORCE BASE

GUAM

FY24 AJJY183012 (P-012)

PDI: NORTH AIRCRAFT PARKING RAMP

SITE & PAVING PLAN - AREA 23

SCALE: AS SHOWN

EPROJECTS NO.: 1665555

CONSTR CONTROL NO.


NAVFAC DRAWING NO. 17361734

SHEET 111 OF 377

CS123

REDESIGN FINAL SUBMITTAL


FILE NAME: U:\BLDG NAVFAC Pacific\03430603 - P-012 North Aircraft Parking Ramp\700 Working Documents\740 Sheets\740.01 Civil\012_1665555_CS124.dwg
LAYOUT NAME: SITE & PAVING PLAN - AREA 24
PLOTTED: 03/09/2026 12:03pm
USER: CameroS

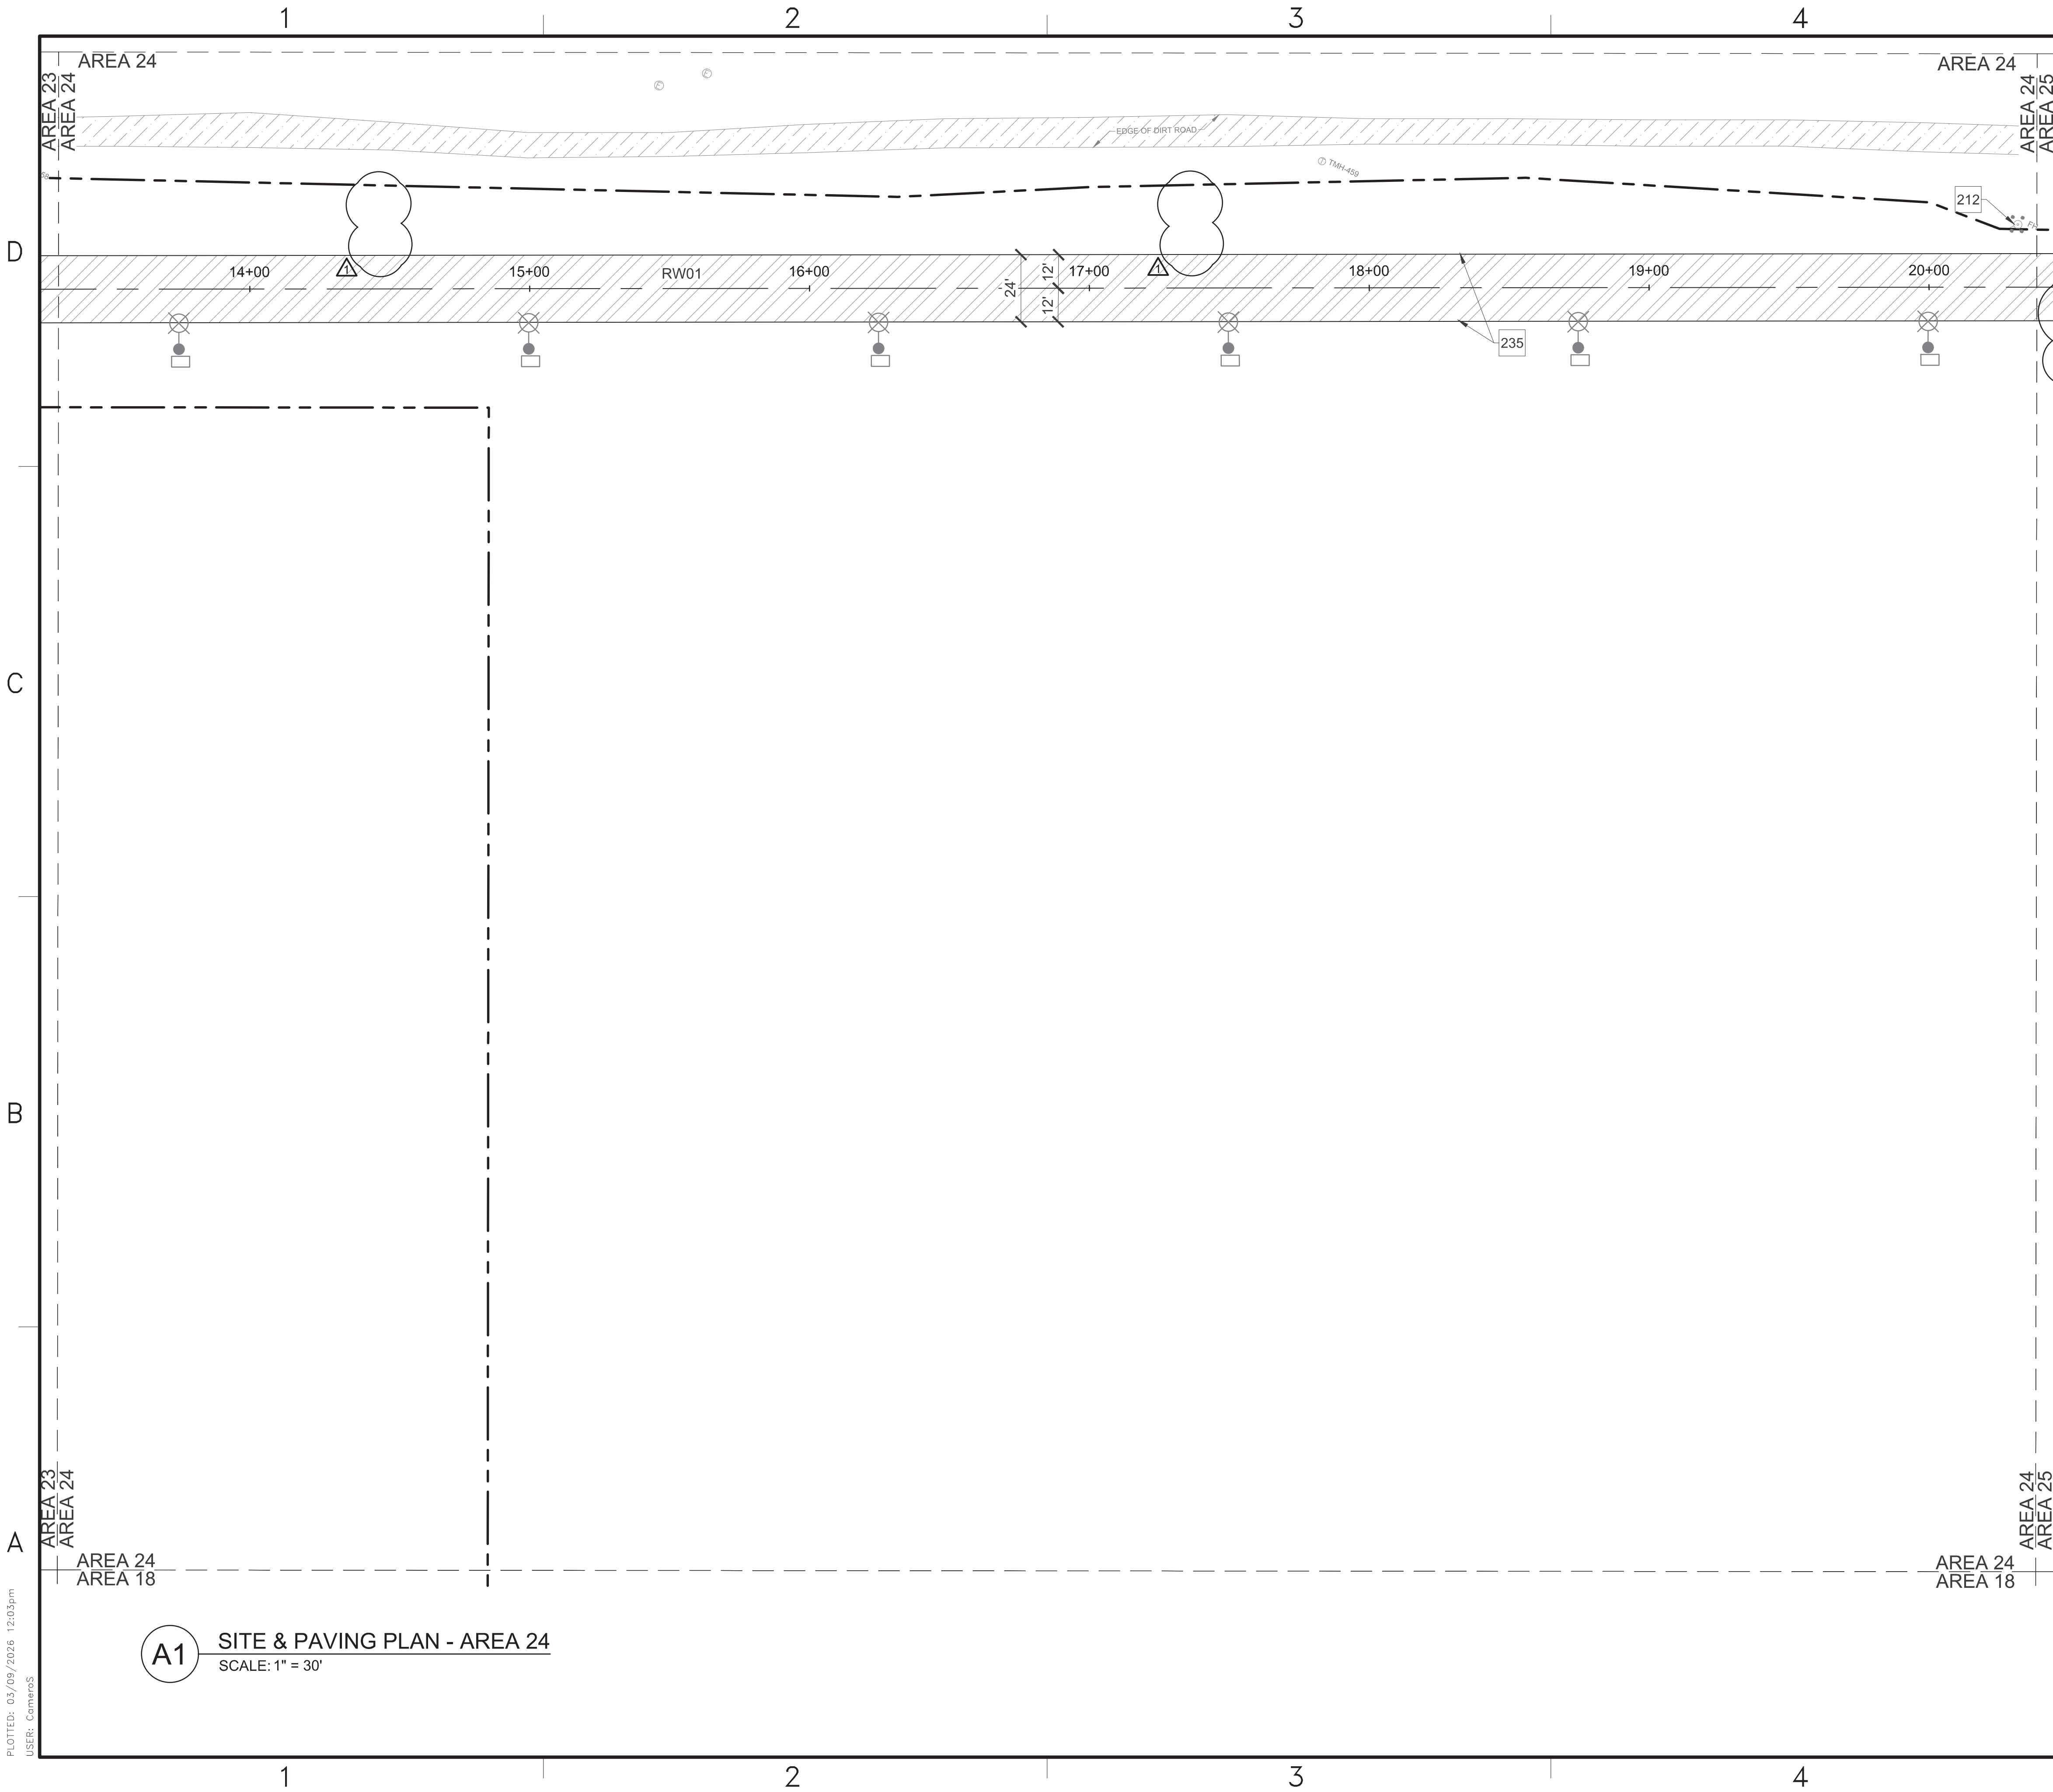

GENERAL NOTES	
A	DIMENSIONS ARE TO BACK OF CURB OR EDGE OF PAVEMENT, UNLESS NOTED OTHERWISE
B	REFER TO ELECTRICAL PLANS FOR SITE LIGHTING INFORMATION
C	REFER TO SHEETS CS130 - CS146 FOR PAVEMENT MARKING PLANS
D	REFER TO SHEETS CS201 - CS211 FOR ROADWAY PROFILES

KEYNOTES	
212	EXISTING FIRE HYDRANT
235	EDGE OF PAVEMENT / ASPHALT TAPER, RE: D4/CS501

LEGEND	
	ASPHALT ROADWAY, RE: C3/CS501
	EXISTING DIRT ROAD
	ROADWAY CENTERLINE
	LIMITS OF DISTURBANCE
	STREET LIGHT POLE, RE: A3/ES503
	EXISTING FIRE HYDRANT
	EXISTING COMMUNICATION MANHOLE
	EXISTING ELECTRICAL MANHOLE
	ELECTRICAL PULL BOX

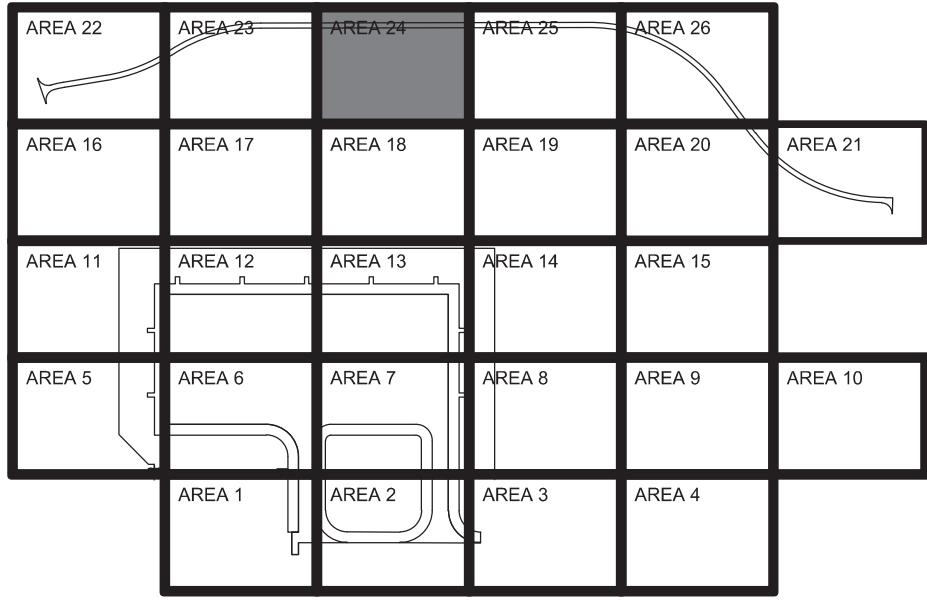

GRAPHIC SCALE

015'30'60'

SCALE: 1"=30'

NORTH ARROW

10-MAR-26

DATE

1

AMEND.002 - REVISED FHS

SYM DESCRIPTION

STATE OF TEXAS

JENNIFER M. HAYNES

90167

LICENSED PROFESSIONAL ENGINEER

3/10/2026

SEAL

JACOBS

BURNS

MCDONNELL

JACOBSBAM, A JOINT VENTURE

1100 NORTH GLEBE ROAD

SUITE 500

ARLINGTON, VA 22201

A/E Contract No. N02742-23-D-0002

A/E Task Order No. N02742-23-D-0002

A/E No. 00000000

A/E INFO

APPROVED

FOR COMMANDER NAVFAC

DATE 04/10/2026

ACTIVITY

AFMISC APPROVAL PER NAVFAC SAT-TO CHECKLIST

SATISFACTORY TO DATE

31 DEC 2026

DES: JMH

DRW: SMC

REV: ATM

PM/DM

KKK

BRANCH MANAGER

SMK

CHIEF ENGINEER

SMK

FIRE PROTECTION

RO

DEPARTMENT OF THE NAVY

NAVAL FACILITIES ENGINEERING SYSTEMS COMMAND

NAVAL FACILITIES ENGINEERING SYSTEMS COMMAND - PACIFIC

JOINT REGION MARIANAS (JRM)

NAVAFAC PACIFIC

ANDERSEN AIR FORCE BASE

GUAM

FY24 AJJY183012 (P-012)

PDI: NORTH AIRCRAFT PARKING RAMP

SITE & PAVING PLAN - AREA 24

SCALE: AS SHOWN

EPROJECTS NO.: 1665555

CONSTR CONTROL NO.


NAVFAC DRAWING NO. 17361735

SHEET 112 OF 377

CS124

REDESIGN FINAL SUBMITTAL


FILE NAME: U:\BLDG\NAVFAC Pacific\03430603 - P-012 North Aircraft Parking Ramp\700 Working Documents\740 Sheets\740.01 Civil\012_1665555_CS125.dwg
LAYOUT NAME: SITE & PAVING PLAN - AREA 25
PLOTTED: 03/09/2026 12:07pm
USER: CameroS

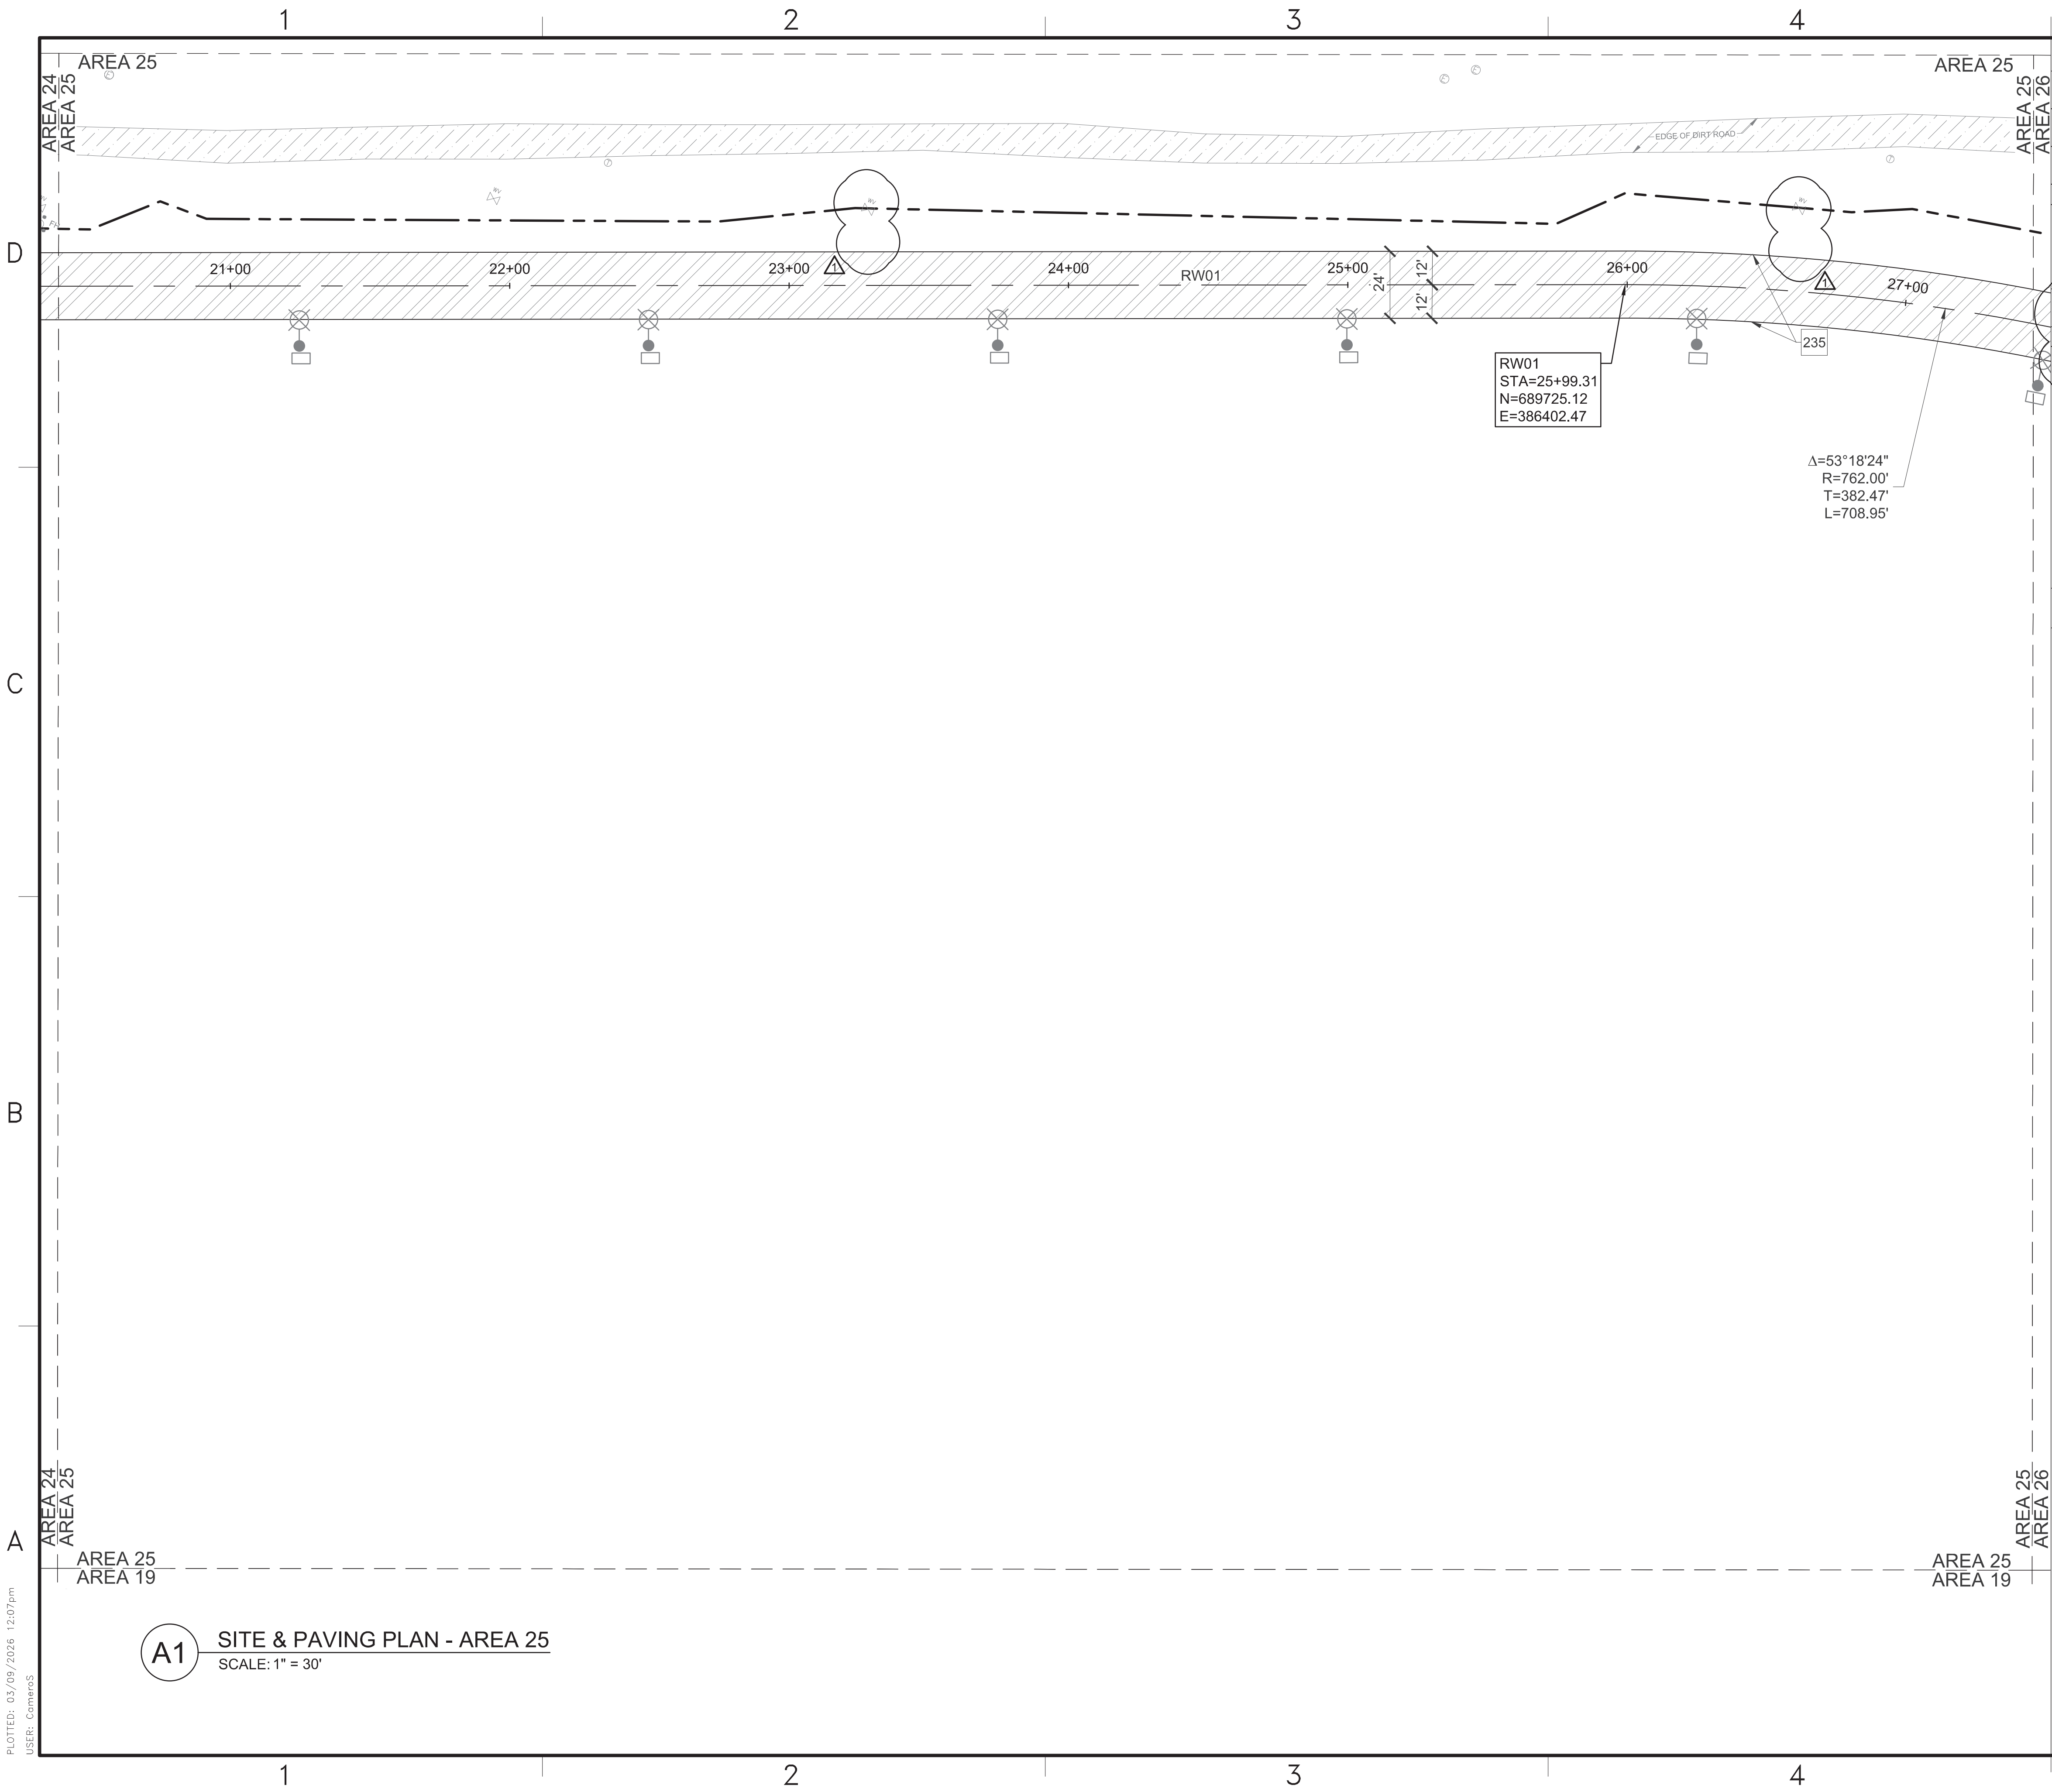

GENERAL NOTES	
A	DIMENSIONS ARE TO BACK OF CURB OR EDGE OF PAVEMENT, UNLESS NOTED OTHERWISE
B	REFER TO ELECTRICAL PLANS FOR SITE LIGHTING INFORMATION
C	REFER TO SHEETS CS130 - CS146 FOR PAVEMENT MARKING PLANS
D	REFER TO SHEETS CS201 - CS211 FOR ROADWAY PROFILES

KEYNOTES	
235	EDGE OF PAVEMENT / ASPHALT TAPER, RE: D4/CS501

LEGEND	
	ASPHALT ROADWAY, RE: C3/CS501
	EXISTING DIRT ROAD
	ROADWAY CENTERLINE
	LIMITS OF DISTURBANCE
	STREET LIGHT POLE, RE: A3/ES503
	EXISTING COMMUNICATION MANHOLE
	EXISTING ELECTRICAL MANHOLE
	EXISTING FIRE HYDRANT
	ELECTRICAL PULL BOX
	EXISTING WATER VALVE

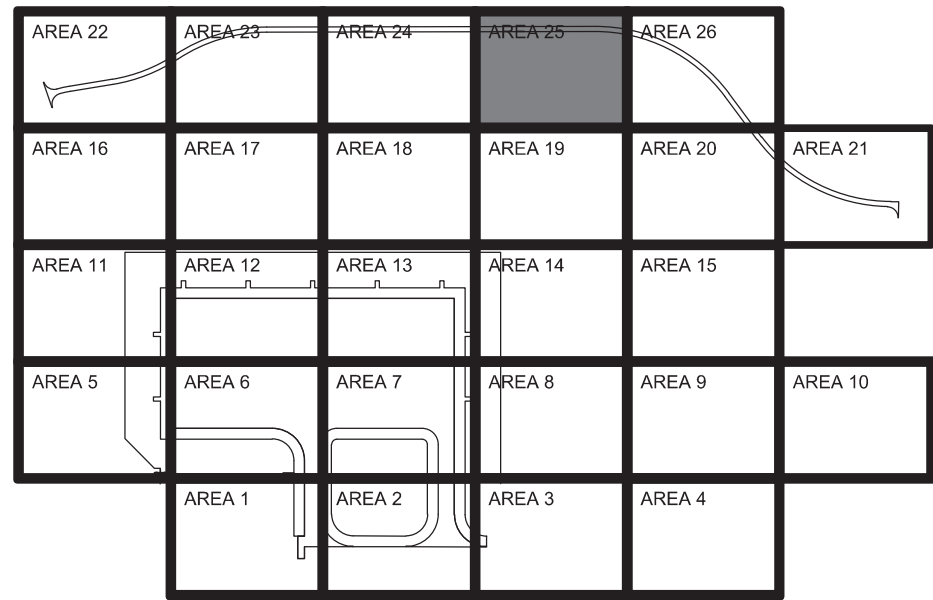

**AREA 25
KEY PLAN**

GRAPHIC SCALE
0 15' 30' 60'
SCALE: 1"=30'


**NORTH
ARROW**
TRUE N

10-MAR-26	DATE
1	AMEND.002-REVISED FHS
SYM	DESCRIPTION
JACOBSBAM, A JOINT VENTURE 1100 NORTH GLEBE ROAD SUITE 500 ARLINGTON, VA 22201 A/E Contract No. N62152-23-D-0002 A/E Task Order No. N62152-23-D-0015 A/E Task Order No. N62152-23-D-0016	
APPROVED Date: 03/09/2026 FOR COMMANDER NAVFAC DATE 04/10/2026	
ACTIVITY AFMISC APPROVAL PER NAVFAC SAT-TO CHECKLIST	
SATISFACTORY TO DATE 31 DEC 2026	
DES: JMH DRW: SMC REV: ATM	
PM/DM KKK	
BRANCH MANAGER SMK	
CHIEF ENGINEER SMK	
FIRE PROTECTION RO	
DEPARTMENT OF THE NAVY NAVAL FACILITIES ENGINEERING SYSTEMS COMMAND NAVAL FACILITIES ENGINEERING SYSTEMS COMMAND - PACIFIC JOINT REGION MARIANAS (JRM) NAVFAC PACIFIC ANDERSEN AIR FORCE BASE GUAM	
FY24 AJY183012 (P-012), PDI: NORTH AIRCRAFT PARKING RAMP SITE & PAVING PLAN - AREA 25	
SCALE: AS SHOWN EPROJECTS NO.: 1665555 CONSTR CONTROL NO.	
NAVFAC DRAWING NO. 17361736	
SHEET 113 OF 377	
CS125	

IF SHEET IS LESS THAN 22" X 34"
REDUCED PRINT. USE GRAPHIC SCALES


REDESIGN FINAL SUBMITTAL

FILE NAME: U:\BLOG\NAVFAC Pacific\03430603 - P-012 North Aircraft Parking Ramp\700 Working Documents\740.01 Sheets\740.01 Civil\012_1665555_CS144.dwg
LAYOUT NAME: PAVEMENT MARKING PLAN - AREA 24
PLOTTED: 03/09/2026 12:11pm
USER: CameroS

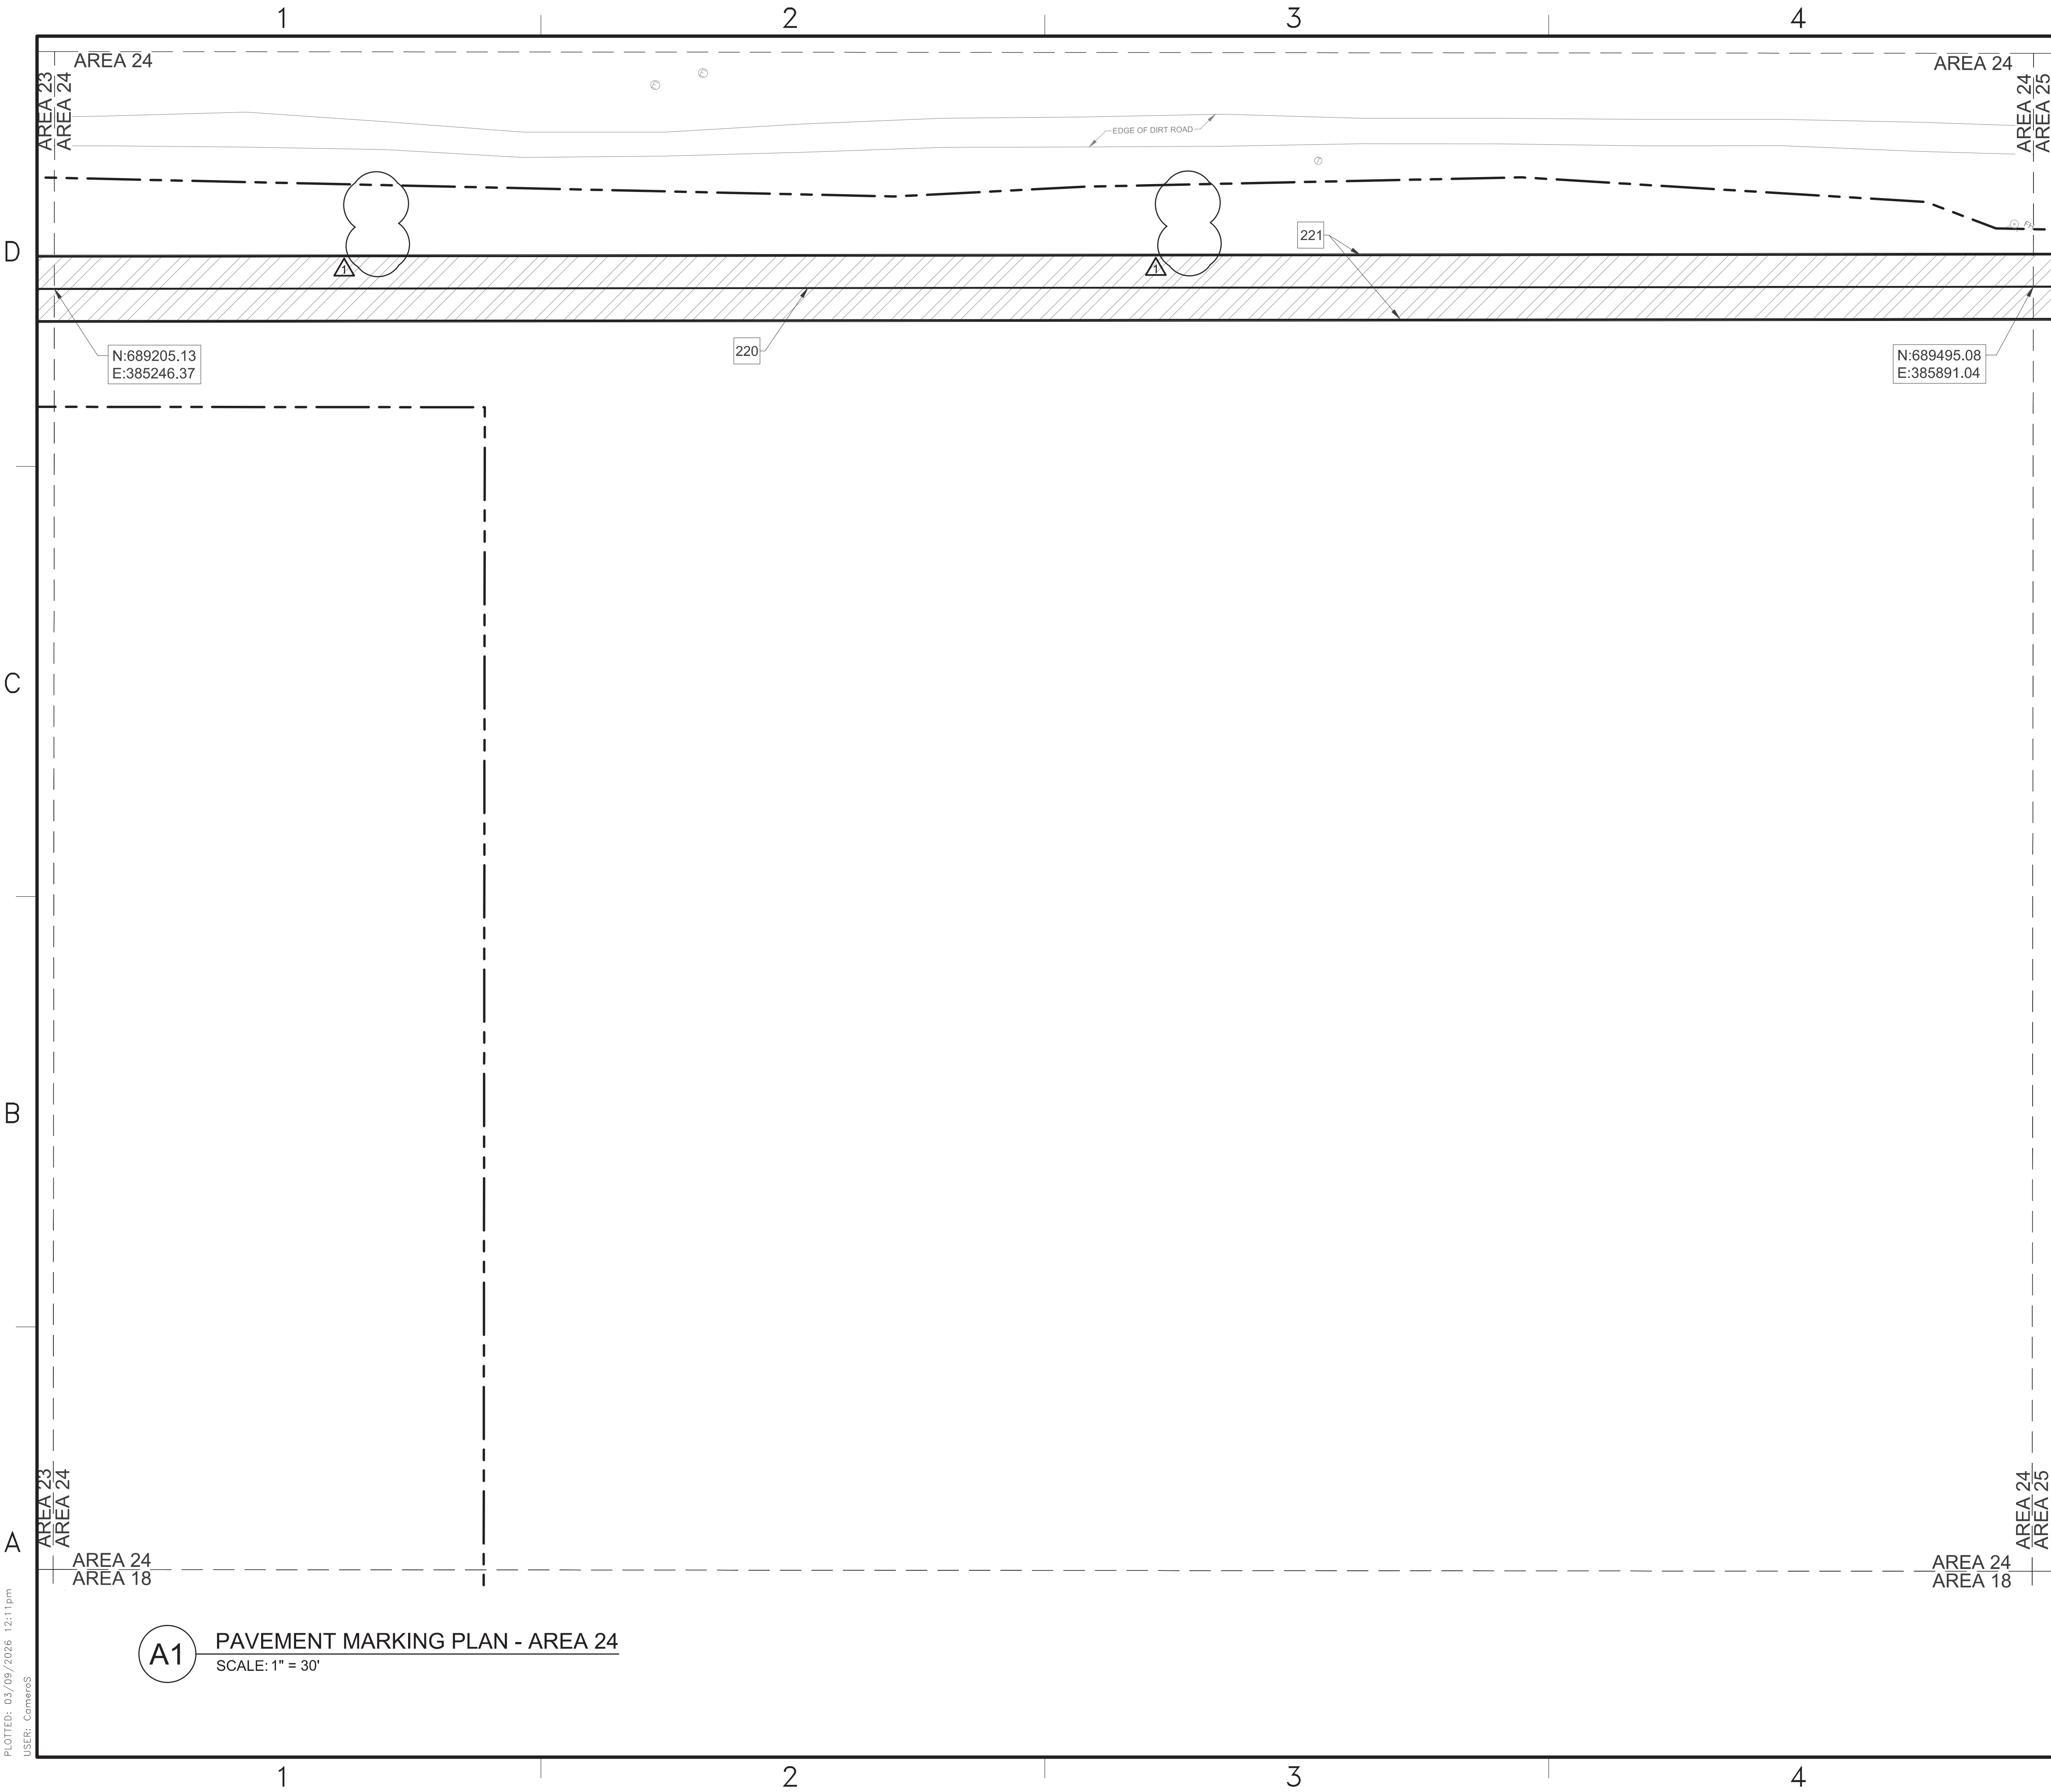

GENERAL NOTES	
A	REFER TO SHEETS CS503 AND CS504 FOR MARKING DETAILS
KEYNOTES	
220	ROADWAY CENTERLINE MARKING, RE: B1/CS503
221	ROADWAY EDGE LINE MARKING, RE: B2/CS503

LEGEND	
	ASPHALT ROADWAY PAVEMENT, RE: C3/CS501
	LIMITS OF DISTURBANCE
	EXISTING FIRE HYDRANT
	EXISTING COMMUNICATION MANHOLE
	EXISTING ELECTRICAL MANHOLE

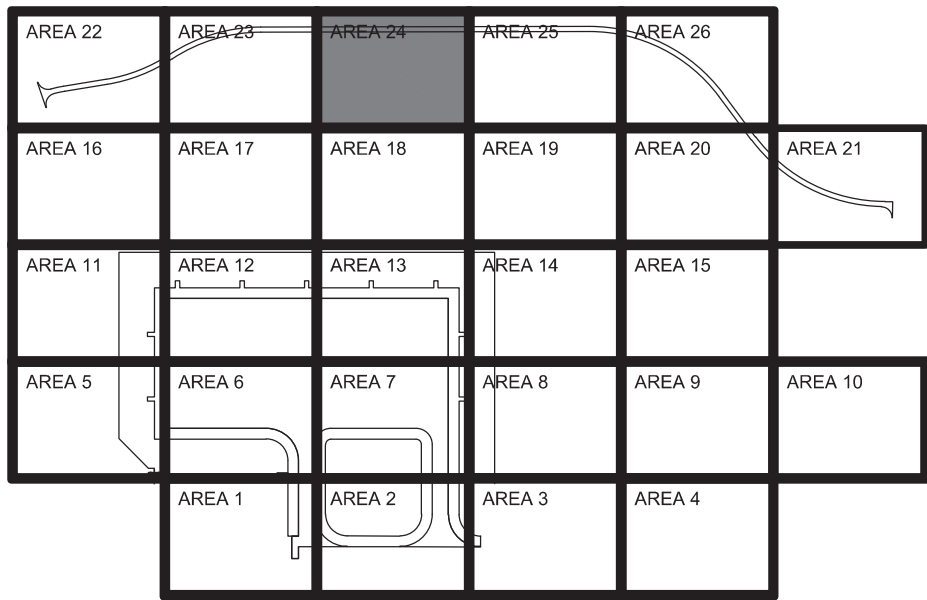


AREA 24 KEY PLAN	
GRAPHIC SCALE	
SCALE: 1"=30'	
NORTH ARROW	

10-MAR-26	DATE
1	AMEND.002 - REVISED FHS
SYM	DESCRIPTION
JACOBSBURN A JOINT VENTURE 1100 NORTH GLEBE ROAD SUITE 500 ARLINGTON, VA 22201 A/E Contract No. N62752-23-0-0002 A/E Task Order No. N62752-23-0-0002 A/E Task Order No. N62752-23-0-0002 A/E Task Order No. N62752-23-0-0002	
APPROVED DATE: 04/10/2026 FOR COMMANDER NAVFAC DATE: 04/10/2026	
ACTIVITY AFMISC APPROVAL PER NAVFAC SAT-TO CHECKLIST	
SATISFACTORY TO DATE 31 DEC 2026	
DES: JMH	DRW: SMC
REV: ATM	PMIDM: KKK
BRANCH MANAGER: SMK	CHIEF ENGINEER: SMK
FIRE PROTECTION: RO	
DEPARTMENT OF THE NAVY NAVAL FACILITIES ENGINEERING SYSTEMS COMMAND NAVAL FACILITIES ENGINEERING SYSTEMS COMMAND - PACIFIC JOINT REGION MARIANAS (JRM) NAVFAC PACIFIC ANDERSEN AIR FORCE BASE GUAM	
FY24 AJY183012 (P-012), PDI: NORTH AIRCRAFT PARKING RAMP PAVEMENT MARKING PLAN - AREA 24	
SCALE: AS SHOWN EPROJECTS NO.: 1665555 CONSTR CONTROL NO.	
NAVFAC DRAWING NO. 17361752	
SHEET 129	OF 377
CS144	

IF SHEET IS LESS THAN 22" X 34"
REDUCED PRINT. USE GRAPHIC SCALES


REDESIGN FINAL SUBMITTAL

FILE NAME: U:\BLDG\NAVFAC Pacific\03430603 - P-012 North Aircraft Parking Ramp\700 Working Documents\740.01 Sheets\740.01 Civil\012_1665555_CS145.dwg
LAYOUT NAME: PAVEMENT MARKING PLAN - AREA 25
PLOTTED: 03/09/2026 12:13pm
USER: CameroS

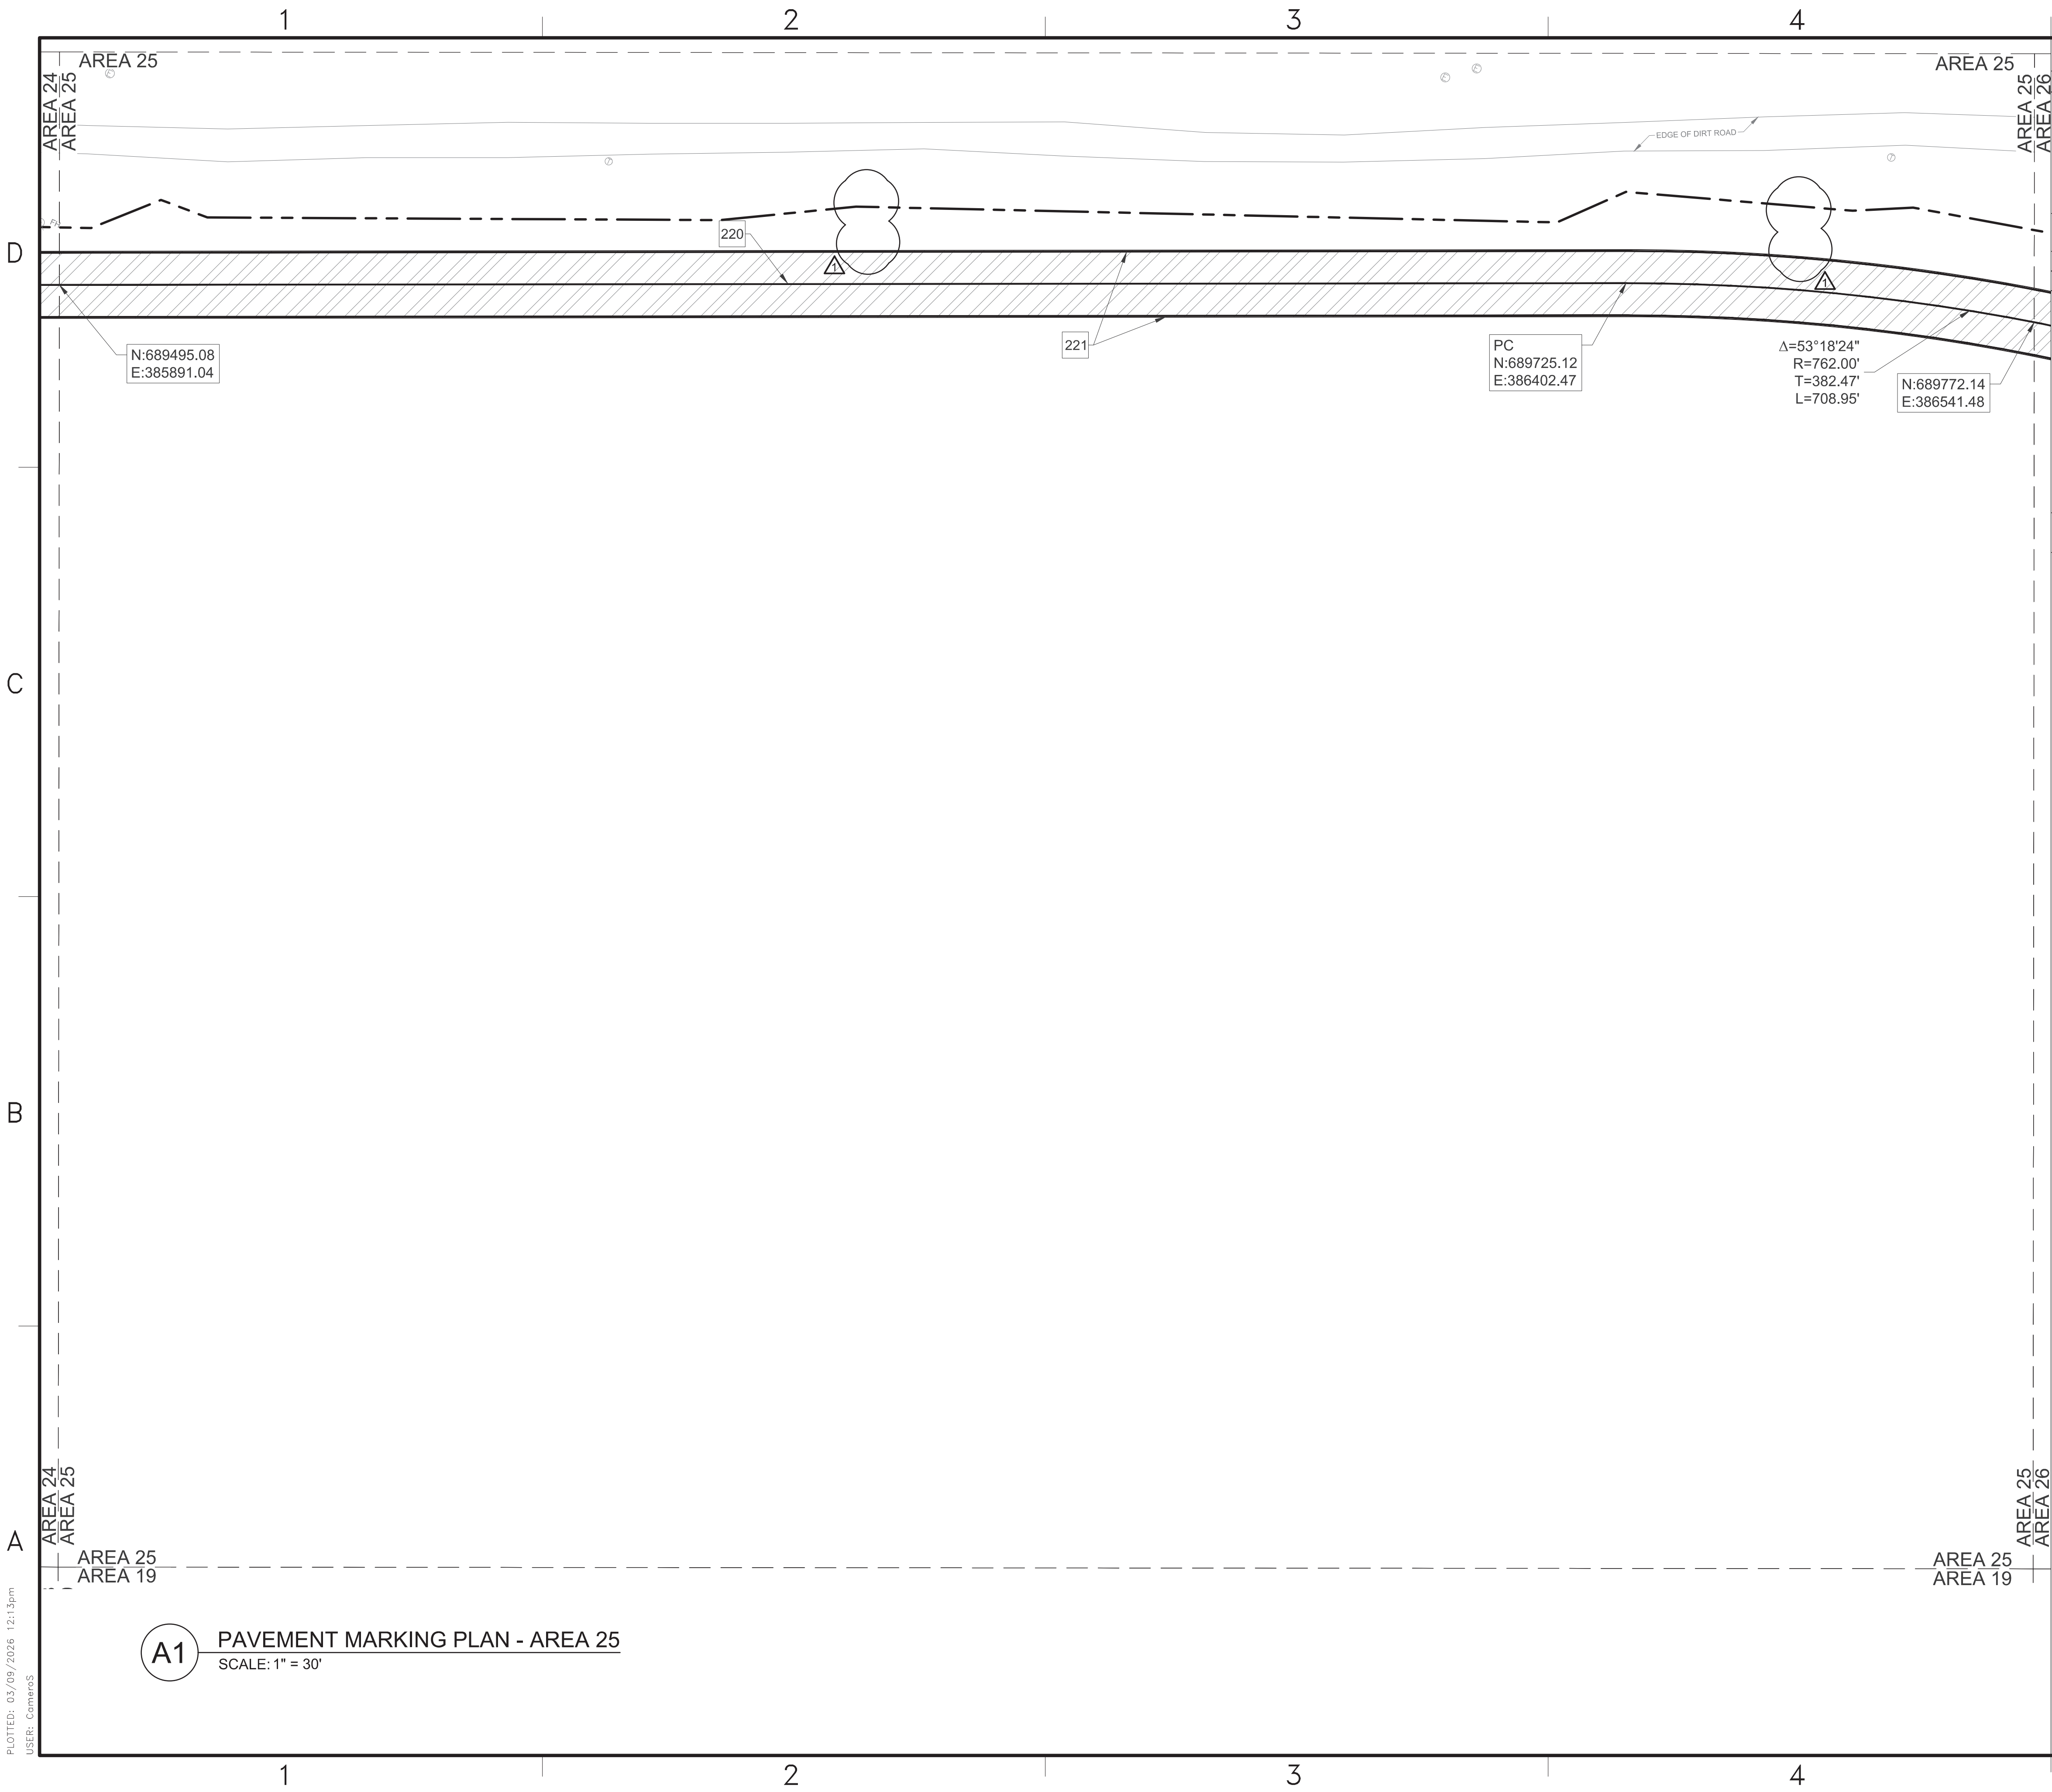

GENERAL NOTES	
A	REFER TO SHEETS CS503 AND CS504 FOR MARKING DETAILS
KEYNOTES	
220	ROADWAY CENTERLINE MARKING, RE: B1/CS503
221	ROADWAY EDGE LINE MARKING, RE: B2/CS503

LEGEND	
	ASPHALT ROADWAY PAVEMENT, RE: C3/CS501
	LIMITS OF DISTURBANCE
	EXISTING FIRE HYDRANT
	EXISTING COMMUNICATION MANHOLE
	EXISTING ELECTRICAL MANHOLE
PC	POINT OF CURVATURE

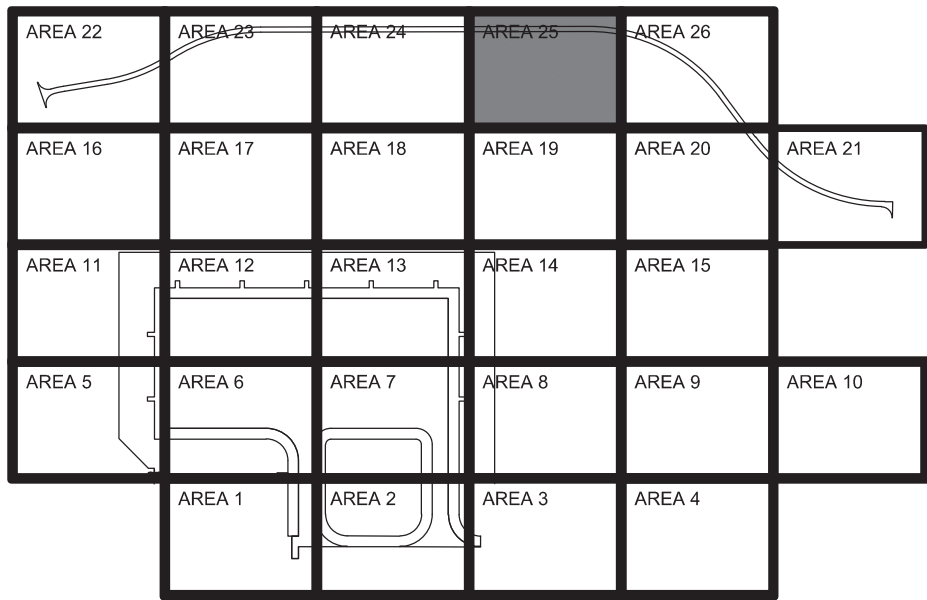

**AREA 25
KEY PLAN**

GRAPHIC SCALE
0 15' 30' 60'
SCALE: 1"=30'

**NORTH
ARROW**
TRUE N

10-MAR-26

DATE

1

AMEND.002 - REVISED FHS

SYM

DESCRIPTION

STATE OF TEXAS

JENNIFER M. HAYNES

90167

LICENSED PROFESSIONAL ENGINEER

3/10/2026

SEAL

JACOBS

BURNS & MCDONNELL

JACOBS&M, A JOINT VENTURE

1100 NORTH GLEBE ROAD

SUITE 500

ARLINGTON, VA 22201

A/E Contract No. N62715-23-0-0002

A/E Task Order No. N62715-23-0-0002

A/E Task Order No. N62715-23-0-0002

A/E Task Order No. N62715-23-0-0002

A/E INFO

APPROVED

FOR COMMANDER NAVFAC DATE 04/10/2026

ACTIVITY

AFMISC APPROVAL PER NAVFAC SAT-TO CHECKLIST

SATISFACTORY TO DATE

31 DEC 2026

DES: JMH

DRW: SMC

REV: ATM

PM/DM

KKK

BRANCH MANAGER

SMK

CHIEF ENGINEER

SMK

FIRE PROTECTION

RO

DEPARTMENT OF THE NAVY

NAVAL FACILITIES ENGINEERING SYSTEMS COMMAND

NAVAL FACILITIES ENGINEERING SYSTEMS COMMAND - PACIFIC

JOINT REGION MARIANAS (JRM)

GUAM

FY24 AJY183012 (P-012)

PDI: NORTH AIRCRAFT PARKING RAMP

PAVEMENT MARKING PLAN - AREA 25

SCALE: AS SHOWN

EPROJECTS NO.: 1665555

CONSTR CONTROL NO.



NAVFAC DRAWING NO. 17361753

SHEET 130 OF 377

CS145

REDESIGN FINAL SUBMITTAL

FILE NAME: U:\BLDG\NAVFAC Pacific\03430603 - P-012 North Aircraft Parking Ramp\700 Working Documents\740.01 Sheets\740.01 Civil\012_1665555_CS202.dwg
LAYOUT NAME: ROADWAY PLAN & PROFILE RW01 - AREA 22 & 23
PLOTTED: 03/09/2026 12:18pm
USER: CameroS

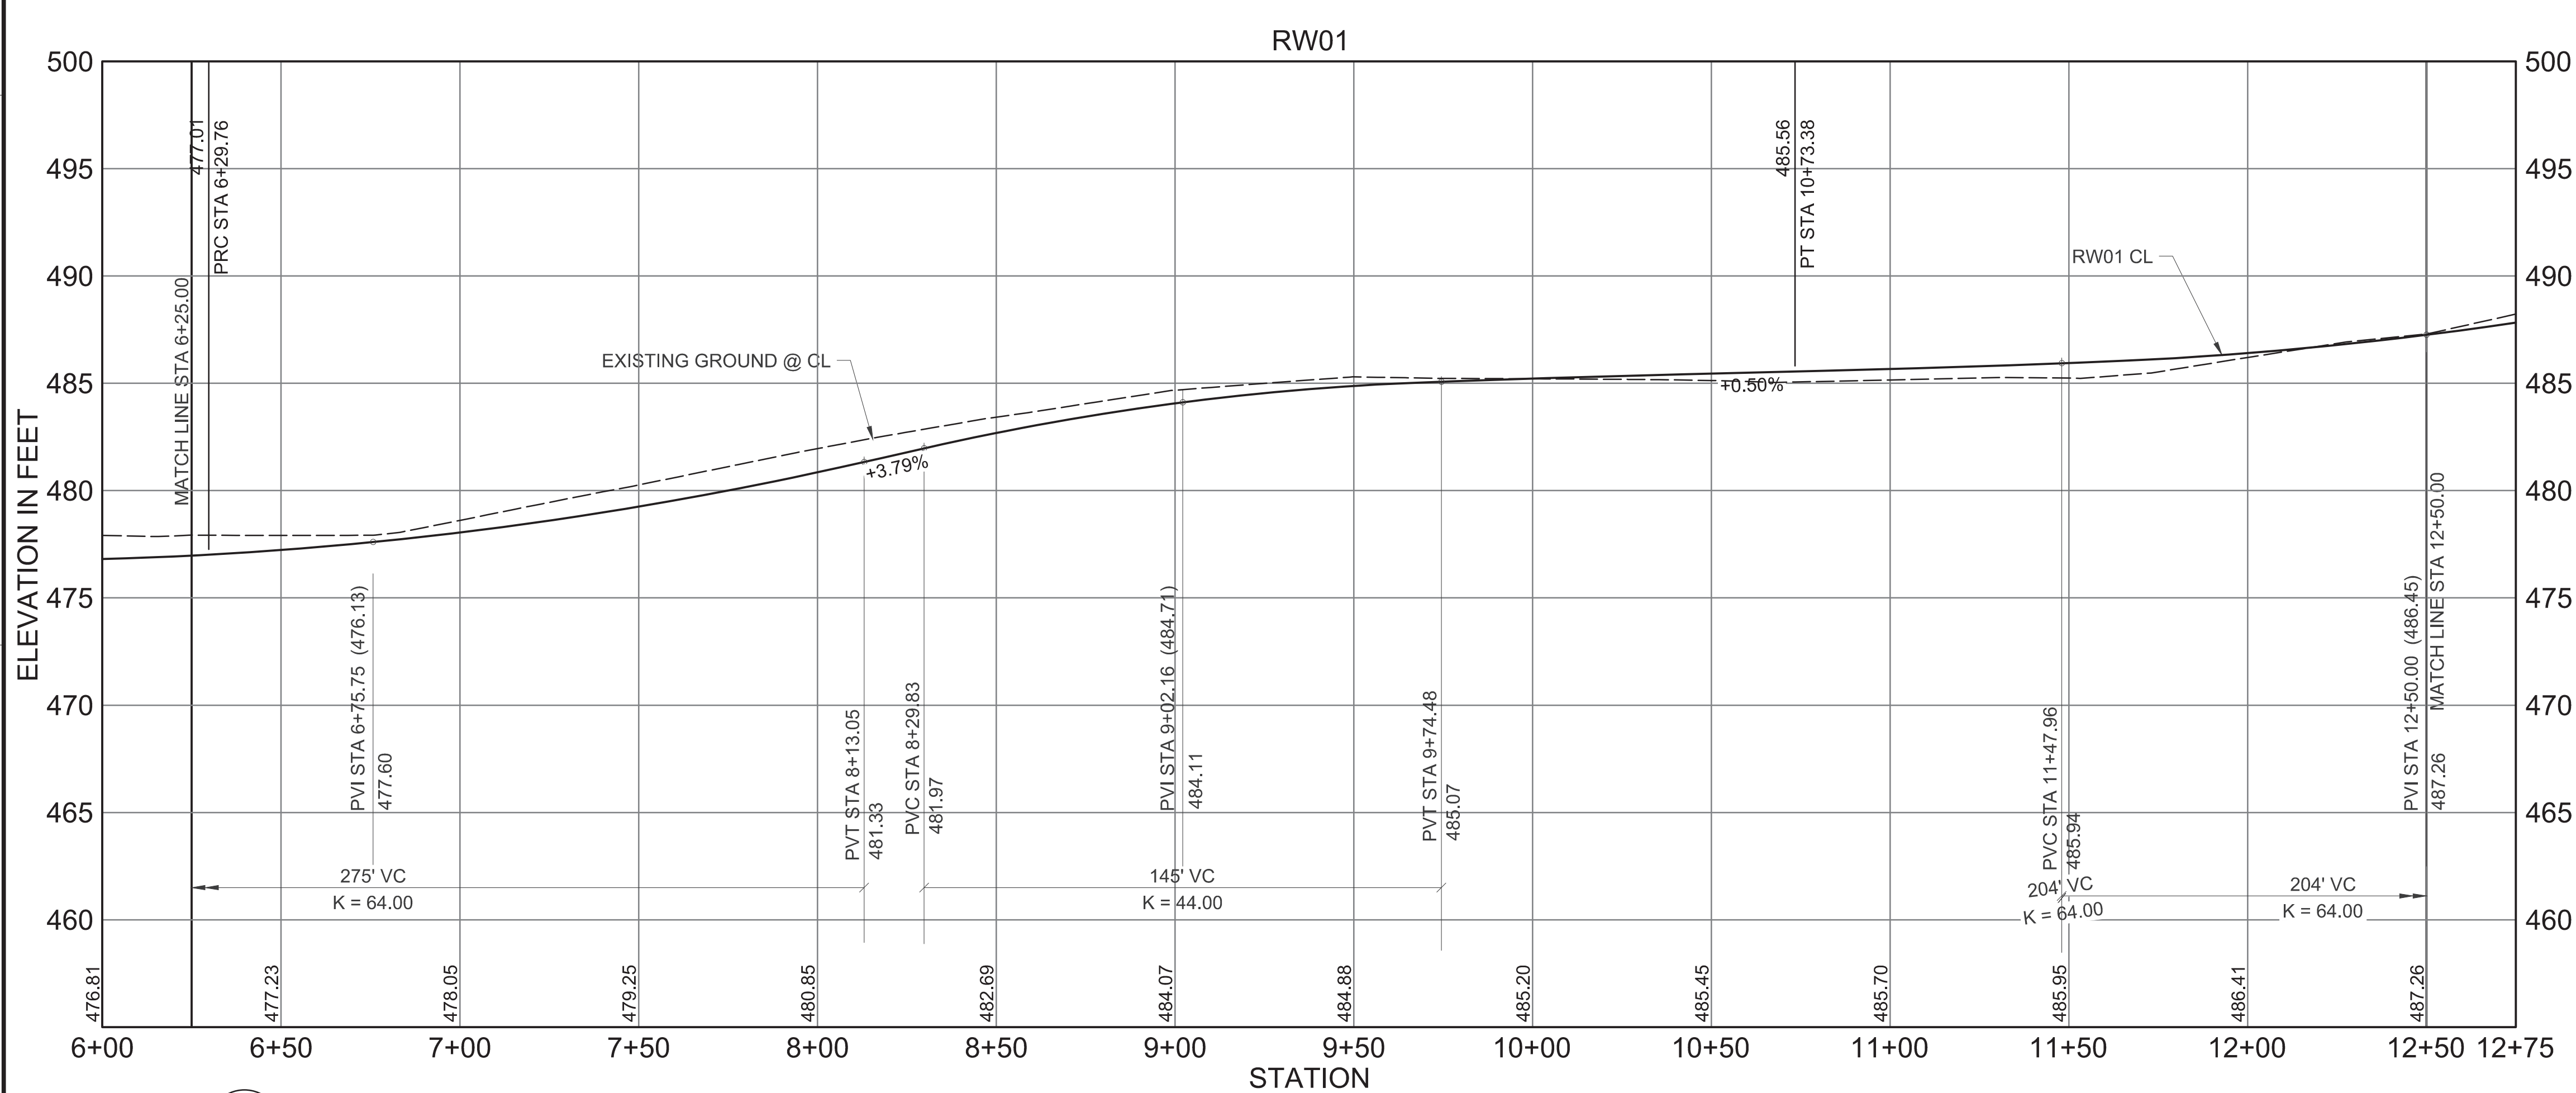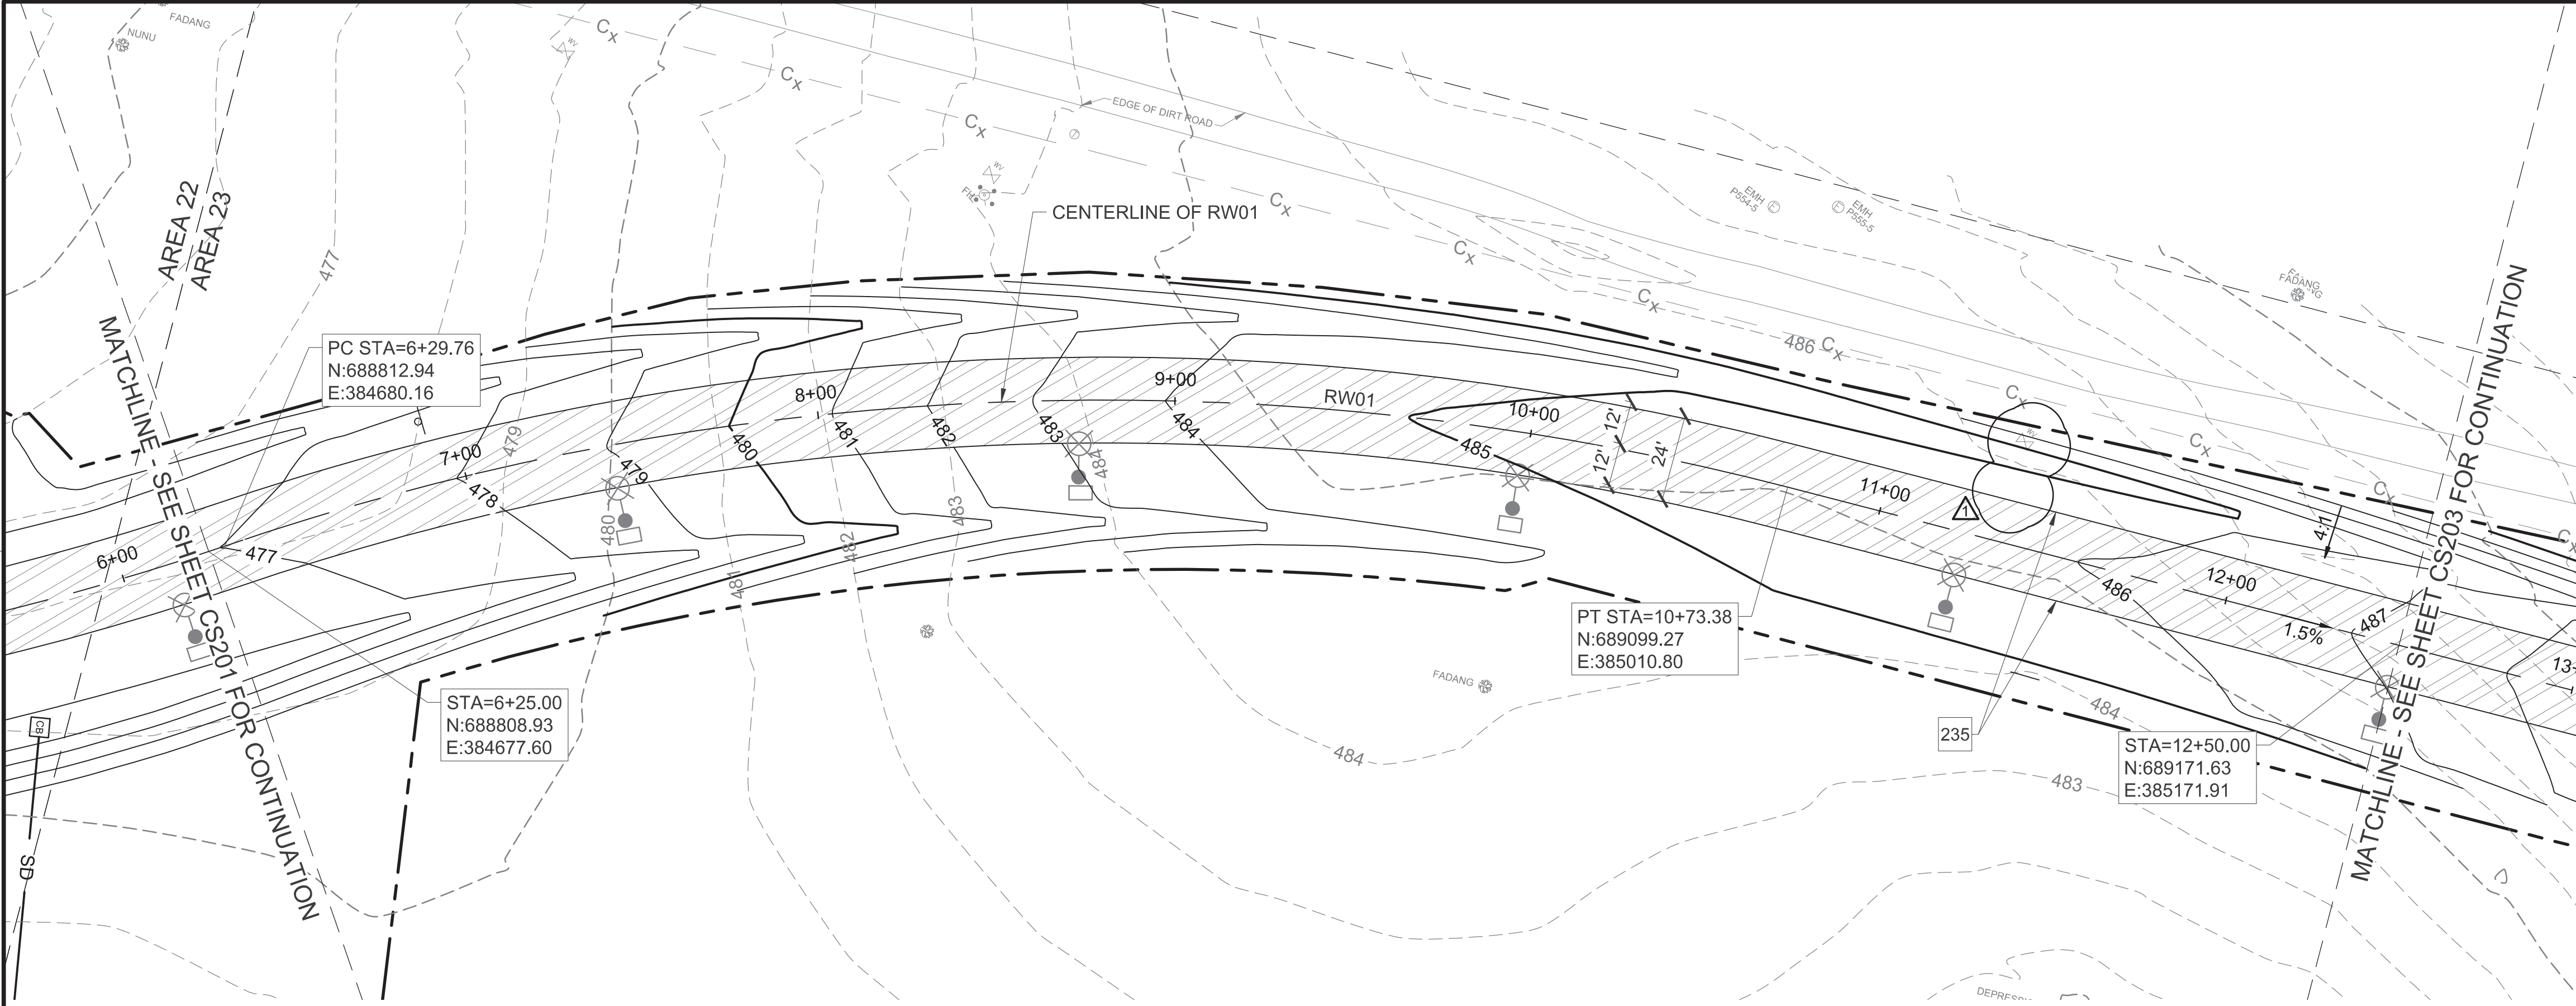

A1 ROADWAY PLAN & PROFILE RW01 STA 6+25-12+50 - AREA 22 & 23
SCALE: HORIZONTAL 1" = 30'
VERTICAL 1" = 5'

GENERAL NOTES
A REFER TO SHEETS CS503 AND CS504 FOR MARKING DETAILS

KEYNOTES
235 EDGE OF PAVEMENT / ASPHALT TAPER, RE: D4/CS501

LEGEND

- ASPHALT ROADWAY, RE: C3/CS501
- LIMITS OF DISTURBANCE
- EXISTING MAJOR CONTOUR
- EXISTING MINOR CONTOUR
- MINOR CONTOUR
- MAJOR CONTOUR
- ROADWAY CENTERLINE
- STREET LIGHT POLE, RE: A3/ES503
- ELECTRICAL PULL BOX
- EXISTING FIRE HYDRANT
- EXISTING WATER VALVE
- EXISTING ELECTRICAL MANHOLE/HANDHOLE
- POINT OF TANGENT
- EXISTING TREE

KEY PLAN

GRAPHIC SCALES
SCALE: 1"=5' SCALE: 1"=30'

NORTH ARROW
TRUE N

STATE OF TEXAS
JENNIFER M. HAYNES
90167
LICENSED PROFESSIONAL ENGINEER
3/10/2026
SEAL

JACOBS **BURNS & MCDONNELL**
JACOBSRAM, A JOINT VENTURE
1100 NORTH GLEBE ROAD
SUITE 500
ARLINGTON, VA 22201
A/E Contract No. 1665555-0002
A/E Task Order No. 1665555-0002
A/E Task Order No. 1665555-0003
A/E Task Order No. 1665555-0004

APPROVED
DATE 04/10/2026
FOR COMMANDER NAVFAC

ACTIVITY
AFMISC APPROVAL PER NAVFAC
SAT-TO CHECKLIST

SATISFACTORY TO DATE 31 DEC 2026

DES: JMH DRW: SMC REV: ATM
PMIDM KKK
BRANCH MANAGER SMK
CHIEF ENGINEER SMK
FIRE PROTECTION RO

NAVAL FACILITIES ENGINEERING SYSTEMS COMMAND
NAVAL FACILITIES ENGINEERING SYSTEMS COMMAND - PACIFIC
NAVFAC PACIFIC
ANDERSEN AIR FORCE BASE
GUAM



FY24 AJJY183012 (P-012),
PDI: NORTH AIRCRAFT PARKING RAMP
ROADWAY PLAN & PROFILE RW01 STA 6+25-12+50 - AREA 22 & 23

SCALE: AS SHOWN
EPROJECTS NO.: 1665555
CONSTR CONTROL NO.
NAVFAC DRAWING NO. 17361756
SHEET 133 OF 377
CS202

IF SHEET IS LESS THAN 22" X 34"
REDUCED PRINT. USE GRAPHIC SCALES

REDESIGN FINAL SUBMITTAL

FILE NAME: U:\BLDG NAVFAC Pacific\03430603 - P-012 North Aircraft Parking Ramp\700 Working Documents\740 Sheets\740.01 Civil\012_1665555_CS203.dwg
LAYOUT NAME: ROADWAY PLAN & PROFILE RW01 - AREA 23 & 24
PLOTED: 03/09/2026 12:25pm
USER: CameroS

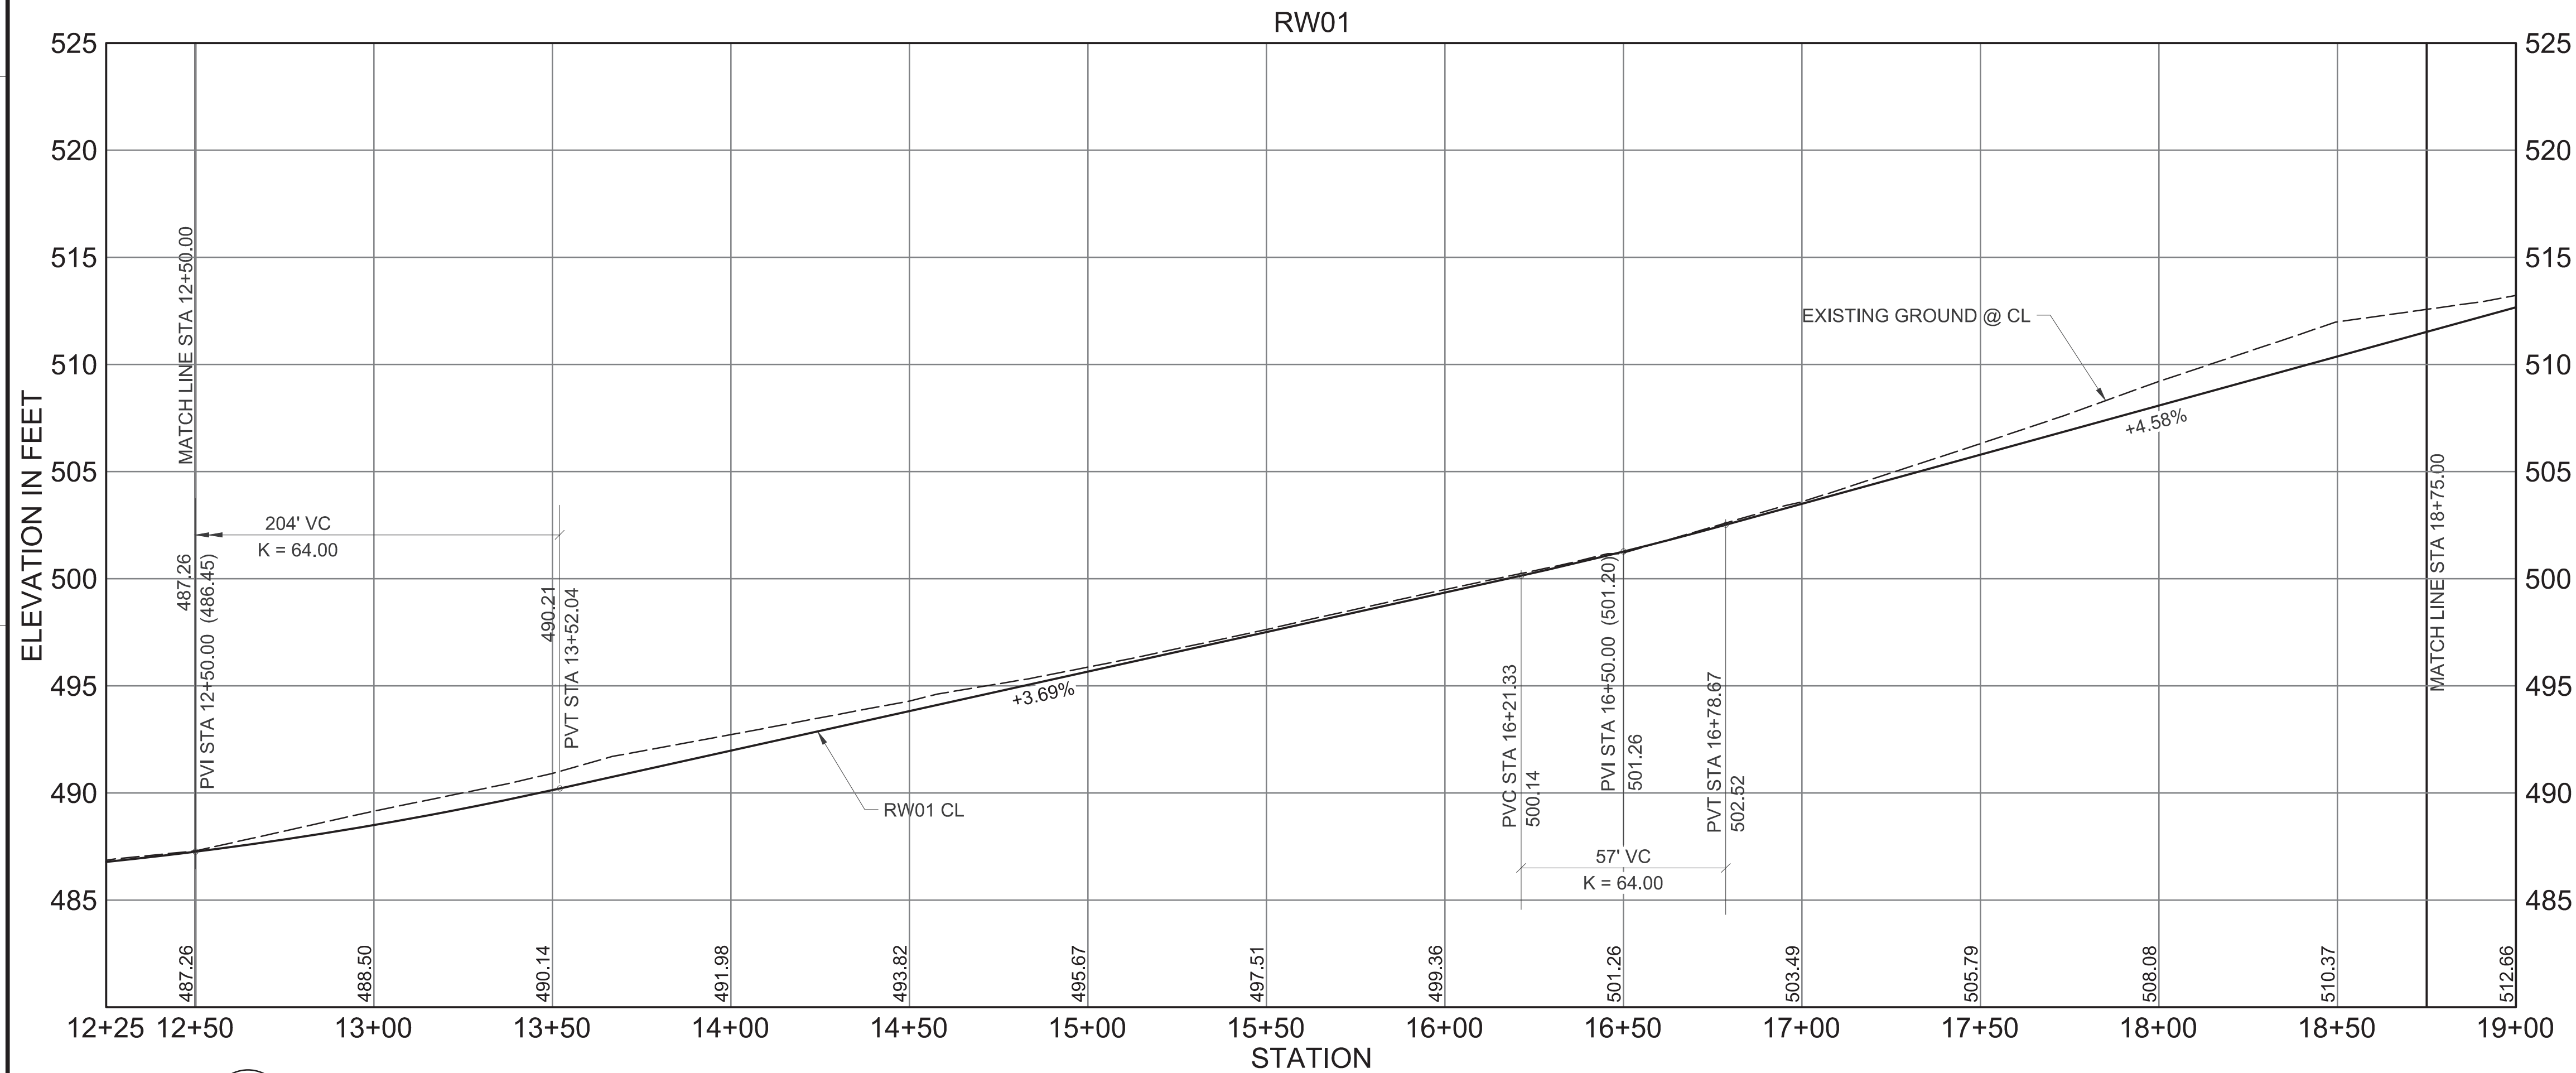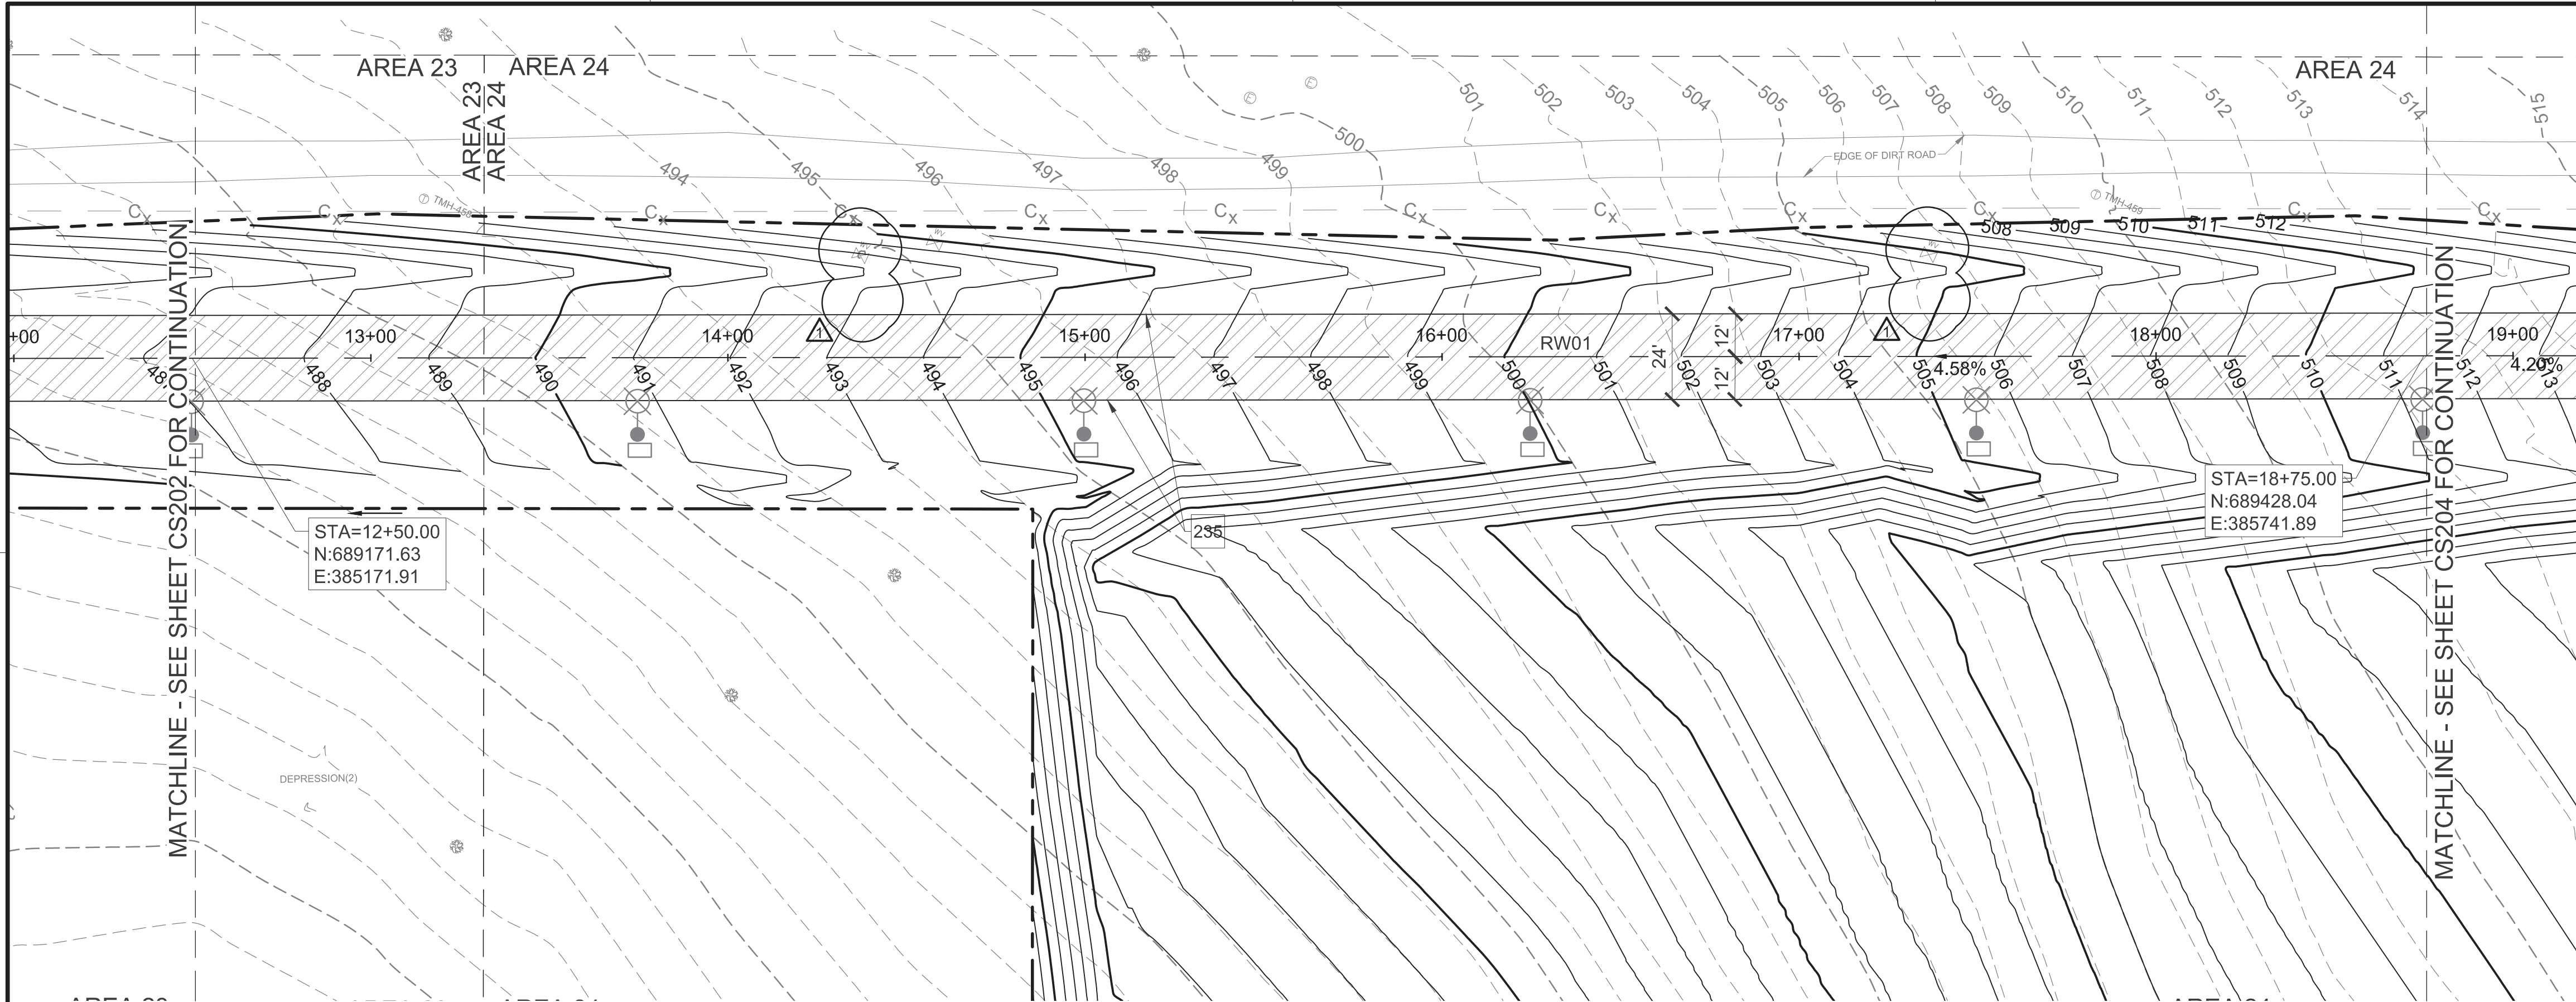

A1 ROADWAY PLAN & PROFILE RW01 STA 12+50-18+75 - AREA 23 & 24
SCALE: HORIZONTAL 1" = 30'
VERTICAL 1" = 5'

GENERAL NOTES

A REFER TO SHEETS CS503 AND CS504 FOR MARKING DETAILS



KEYNOTES

235 EDGE OF PAVEMENT / ASPHALT TAPER, RE: D4/CS501

LEGEND

- ASPHALT ROADWAY, RE: C3/CS501
- LIMITS OF DISTURBANCE
- EXISTING MAJOR CONTOUR
- EXISTING MINOR CONTOUR
- EXISTING UNDERGROUND COMM.
- MINOR CONTOUR
- MAJOR CONTOUR
- ROADWAY CENTERLINE
- STREET LIGHT POLE, RE: A3/ES503
- ELECTRICAL PULL BOX
- EXISTING TREE
- EXISTING COMMUNICATION MANHOLE

KEY PLAN

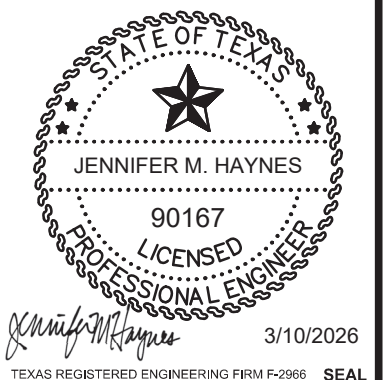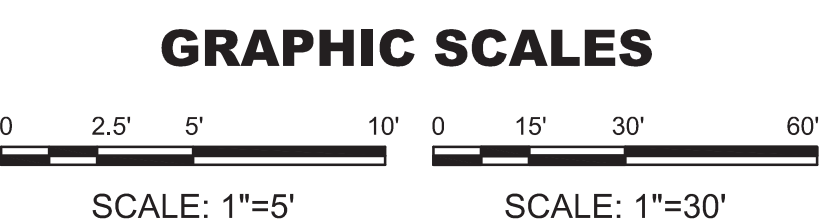

APPROVED
FOR COMMANDER NAVFAC DATE 04/10/2026

ACTIVITY
AFMISC APPROVAL PER NAVFAC
SAT-TO CHECKLIST

SATISFACTORY TO DATE 31 DEC 2026

DES: JMH DRW: SMC REV: ATM

PM/DM KKK

BRANCH MANAGER SMK

CHIEF ENGINEER SMK

FIRE PROTECTION RO

GUAM

NAVAL FACILITIES ENGINEERING SYSTEMS COMMAND

NAVAL FACILITIES ENGINEERING SYSTEMS COMMAND - PACIFIC

JOINT REGION MARIANAS (JRM)

ANDERSEN AIR FORCE BASE

FY24 AUJY183012 (P-012)

PDI: NORTH AIRCRAFT PARKING RAMP

ROADWAY PLAN & PROFILE RW01 STA 12+50-18+75 - AREA 23 & 24

SCALE: AS SHOWN

EPROJETS NO.: 1665555



CONSTR CONTROL NO.

NAVFAC DRAWING NO. 17361757

SHEET 134 OF 377

CS203

FILE NAME: U:\BLOG\NAVFAC Pacific\03430603 - P-012 North Aircraft Parking Ramp\700 Working Documents\740 Sheets\740.01 Civil\012_1665555_CS204.dwg
LAYOUT NAME: ROADWAY PLAN & PROFILE RW01 - AREA 24 & 25
PLOTTED: 03/09/2026 1:22pm
USER: CameroS

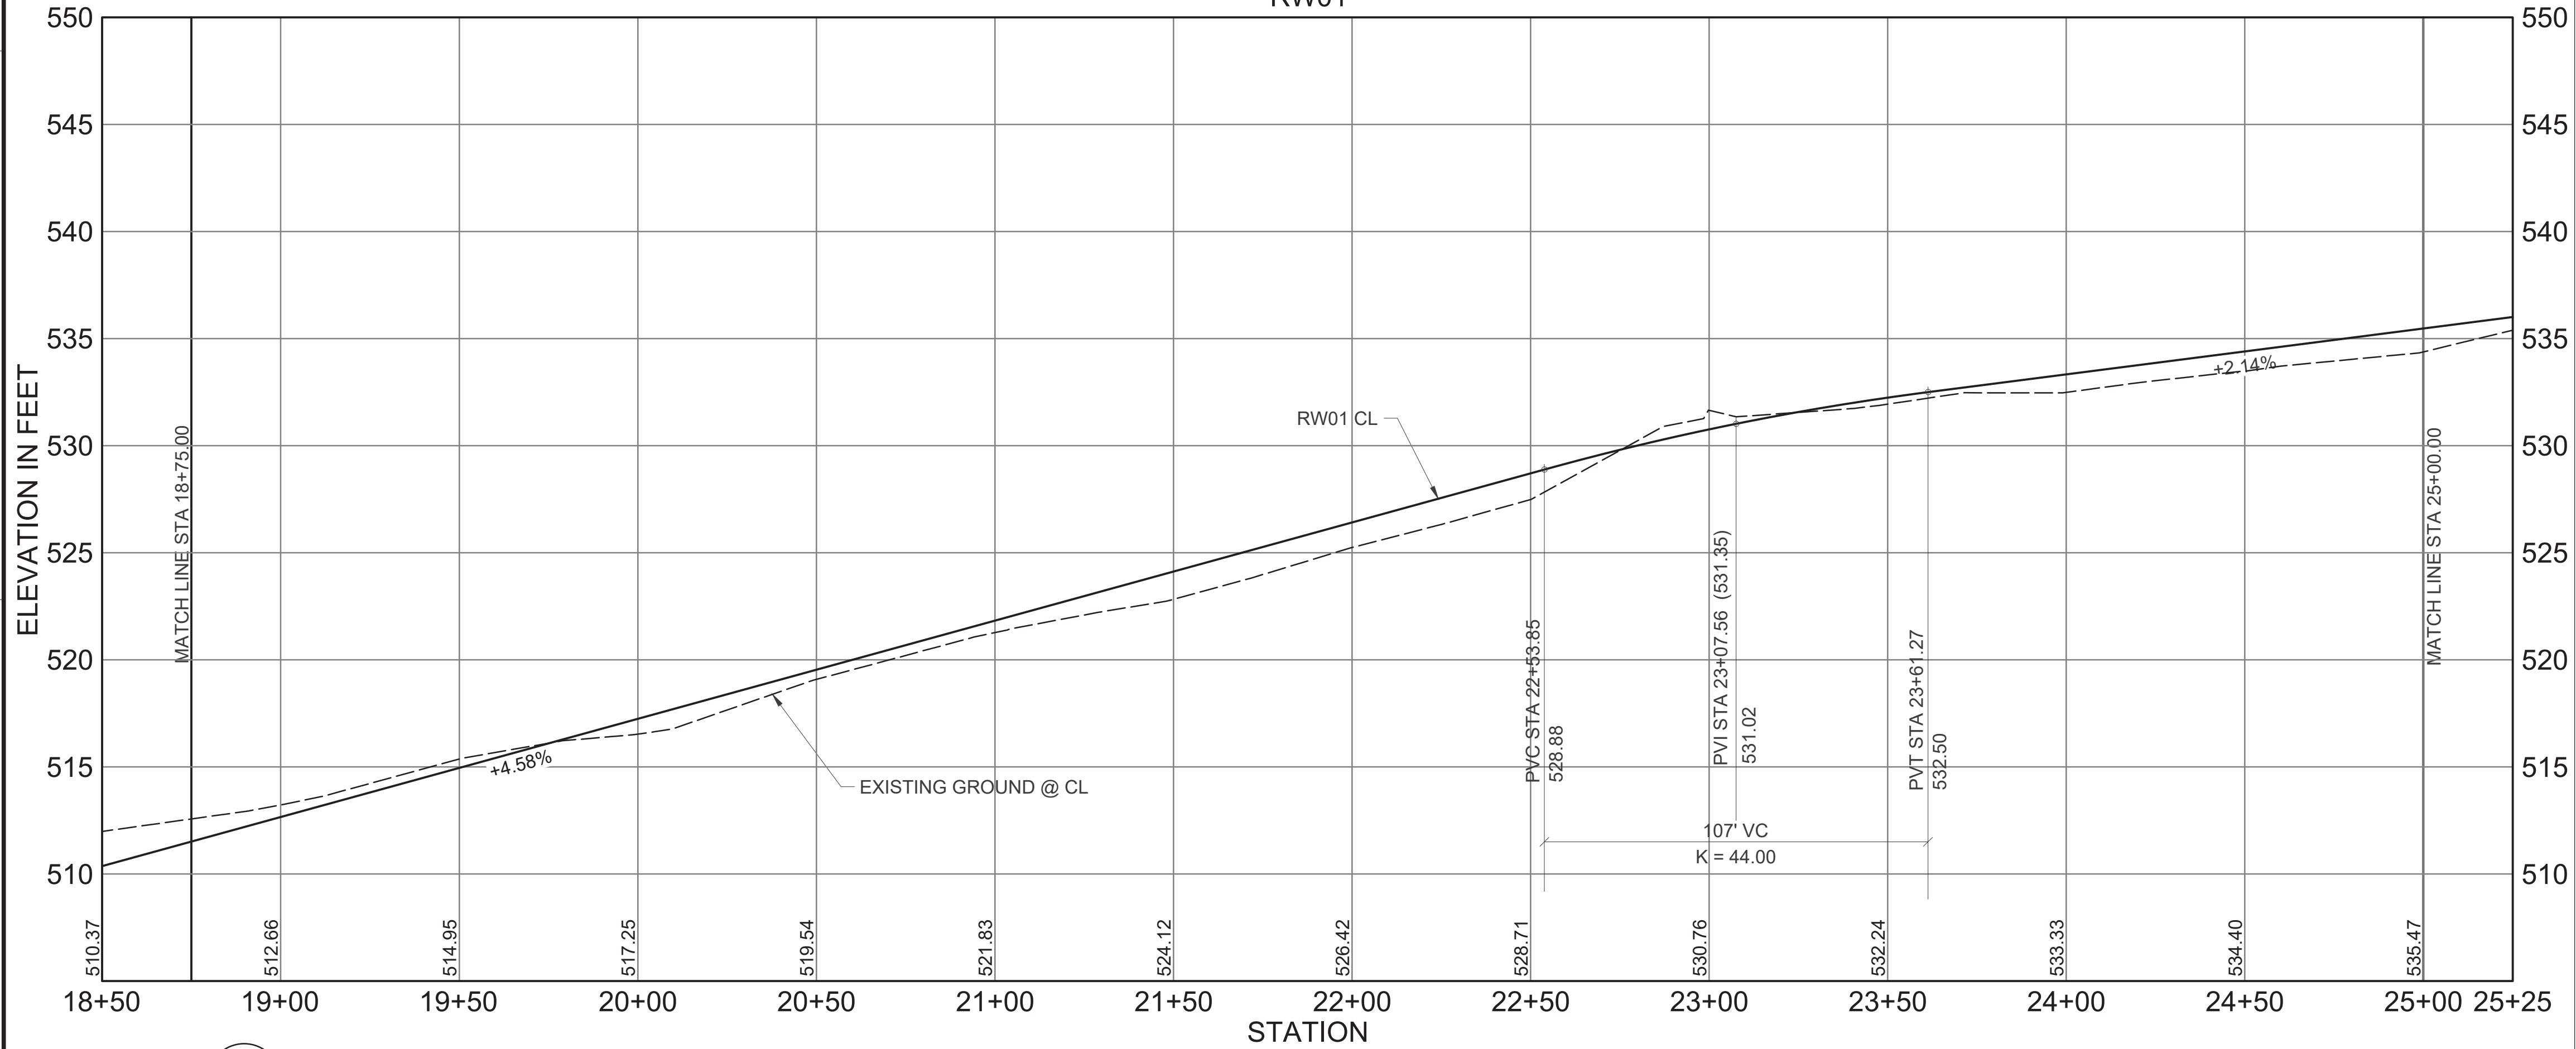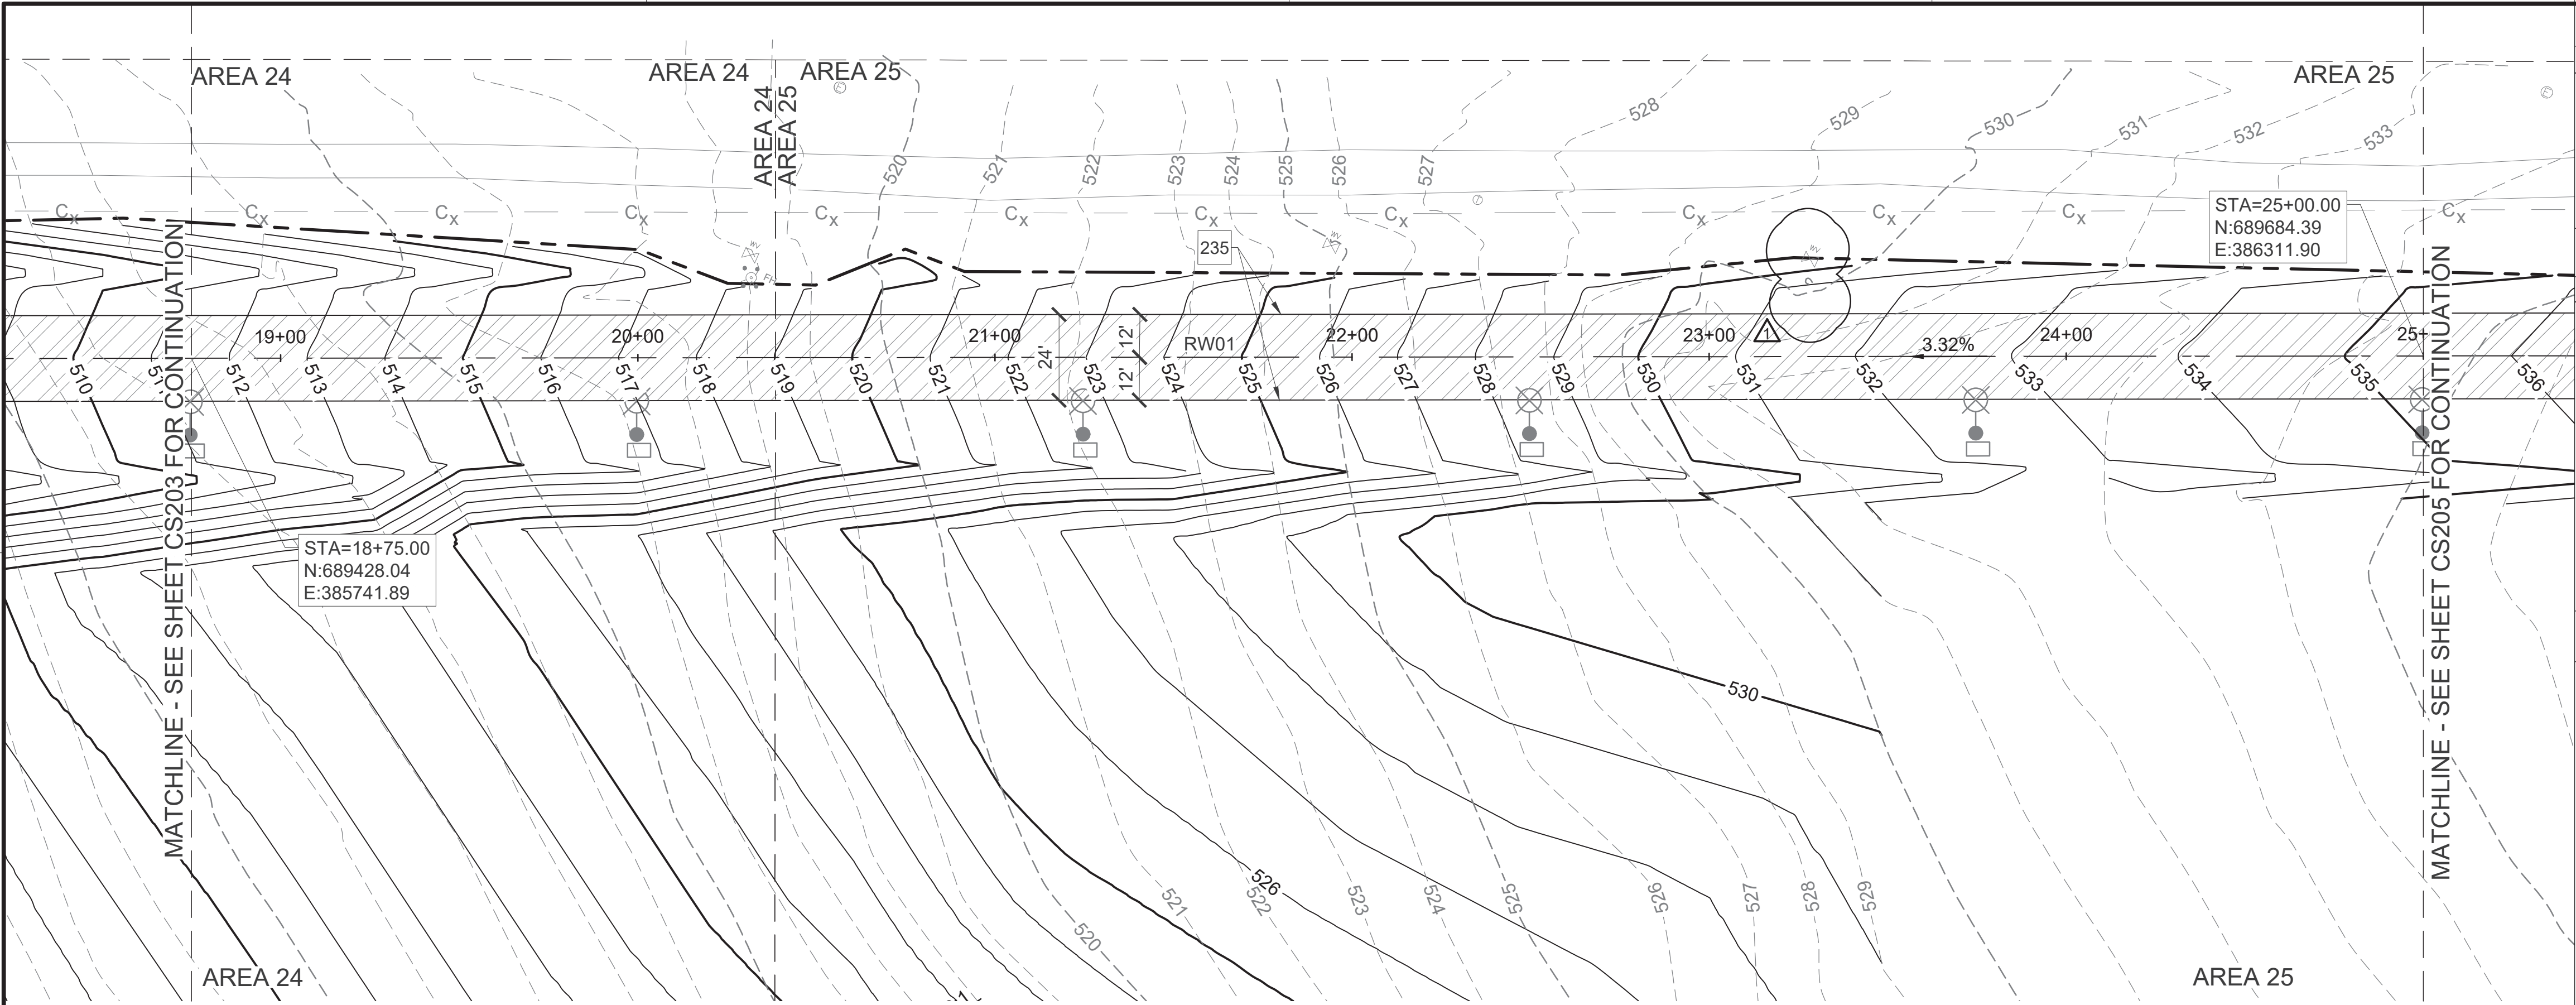

A1 ROADWAY PLAN & PROFILE RW01 STA 18+75-25+00 - AREA 24 & 25
SCALE: HORIZONTAL 1" = 30'
VERTICAL 1" = 5'

GENERAL NOTES
A REFER TO SHEETS CS503 AND CS504 FOR MARKING DETAILS

KEYNOTES
235 EDGE OF PAVEMENT / ASPHALT TAPER, RE: D4/CS501


LEGEND

- ASPHALT ROADWAY, RE: C3/CS501
- LIMITS OF DISTURBANCE
- EXISTING MAJOR CONTOUR
- EXISTING MINOR CONTOUR
- EXISTING UNDERGROUND COMM.
- MINOR CONTOUR
- MAJOR CONTOUR
- ROADWAY CENTERLINE
- STREET LIGHT POLE, RE: A3/ES503
- ELECTRICAL PULL BOX
- EXISTING FIRE HYDRANT
- EXISTING WATER VALVE
- EXISTING COMMUNICATION MANHOLE

KEY PLAN

GRAPHIC SCALES
SCALE: 1"=5' SCALE: 1"=30'

NORTH ARROW
TRUE NORTH

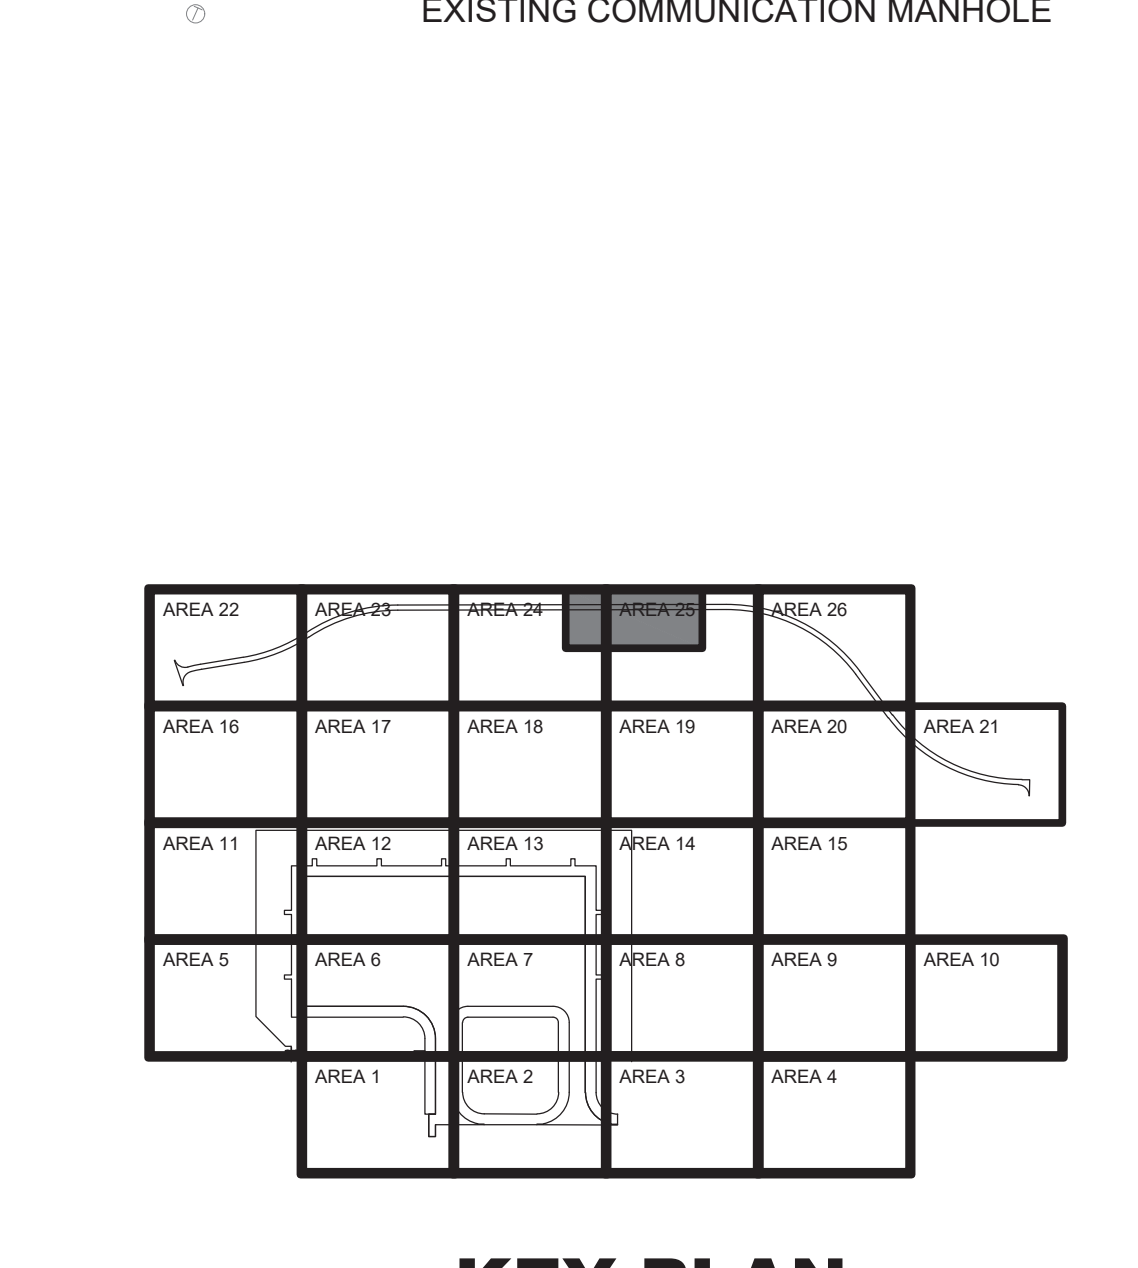

CS204

REDESIGN FINAL SUBMITTAL

1	AMEND 0002 - REVISED FHS	01-MAR-26	DATE
1	DESCRIPTION		

APPROVED
FOR COMMANDER NAVFAC DATE 04/10/2026

ACTIVITY
AFMISC APPROVAL PER NAVFAC SAT-TO CHECKLIST

SATISFACTORY TO DATE 31 DEC 2025

DES: JMH DRW: SMC REV: ATM

PM/DIM KKK

BRANCH MANAGER SMK

CHIEF ENGINEER SMK

FIRE PROTECTION RO

DEPARTMENT OF THE NAVY
NAVAL FACILITIES ENGINEERING SYSTEMS COMMAND
NAVAL FACILITIES ENGINEERING SYSTEMS COMMAND - PACIFIC
NAVFAC PACIFIC
ANDERSEN AIR FORCE BASE

JOINT REGION MARIANAS (JRM)
GUAM

FY24 AJJY183012 (P-012),
PDI: NORTH AIRCRAFT PARKING RAMP
ROADWAY PLAN & PROFILE RW01 STA 18+75-25+00 - AREA 24 & 25

SCALE: AS SHOWN



PROJECTS NO.: 1665555

CONSTR CONTROL NO.

NAVFAC DRAWING NO. 17361758

SHEET 135 OF 377

FILE NAME: U:\BLOG\NAVFAC Pacific\03430603 - P-012 North Aircraft Parking Ramp\700 Working Documents\740 Sheets\740.01 Civil\01012_1665555_CS205.dwg
LAYOUT NAME: SITE & PAVING PLAN - AREA 26
PLOTED: 03/09/2026 1:34pm
USER: CameroS

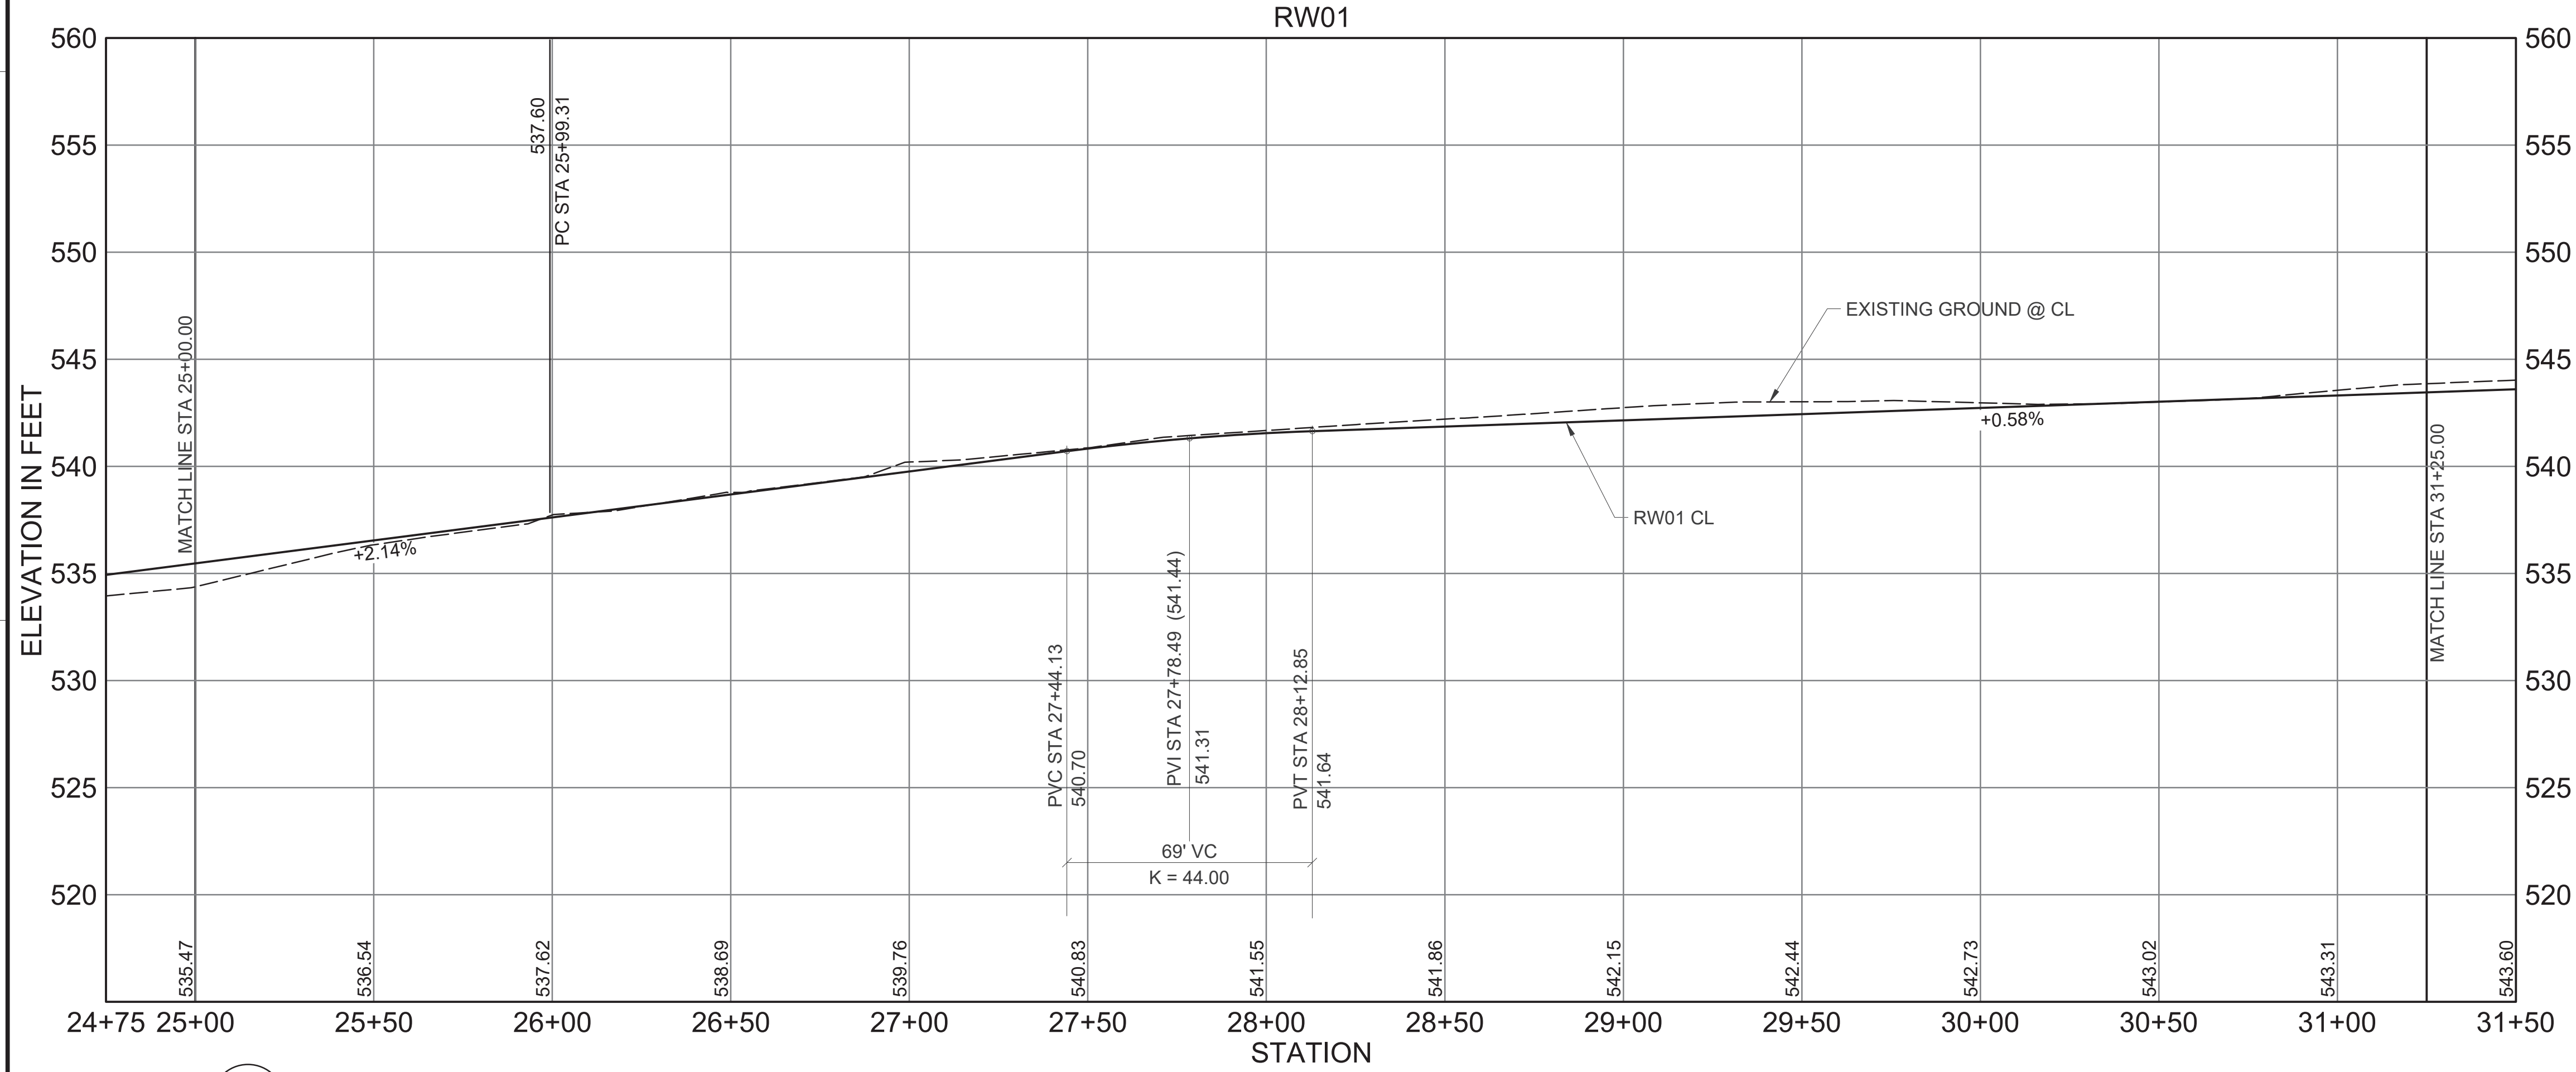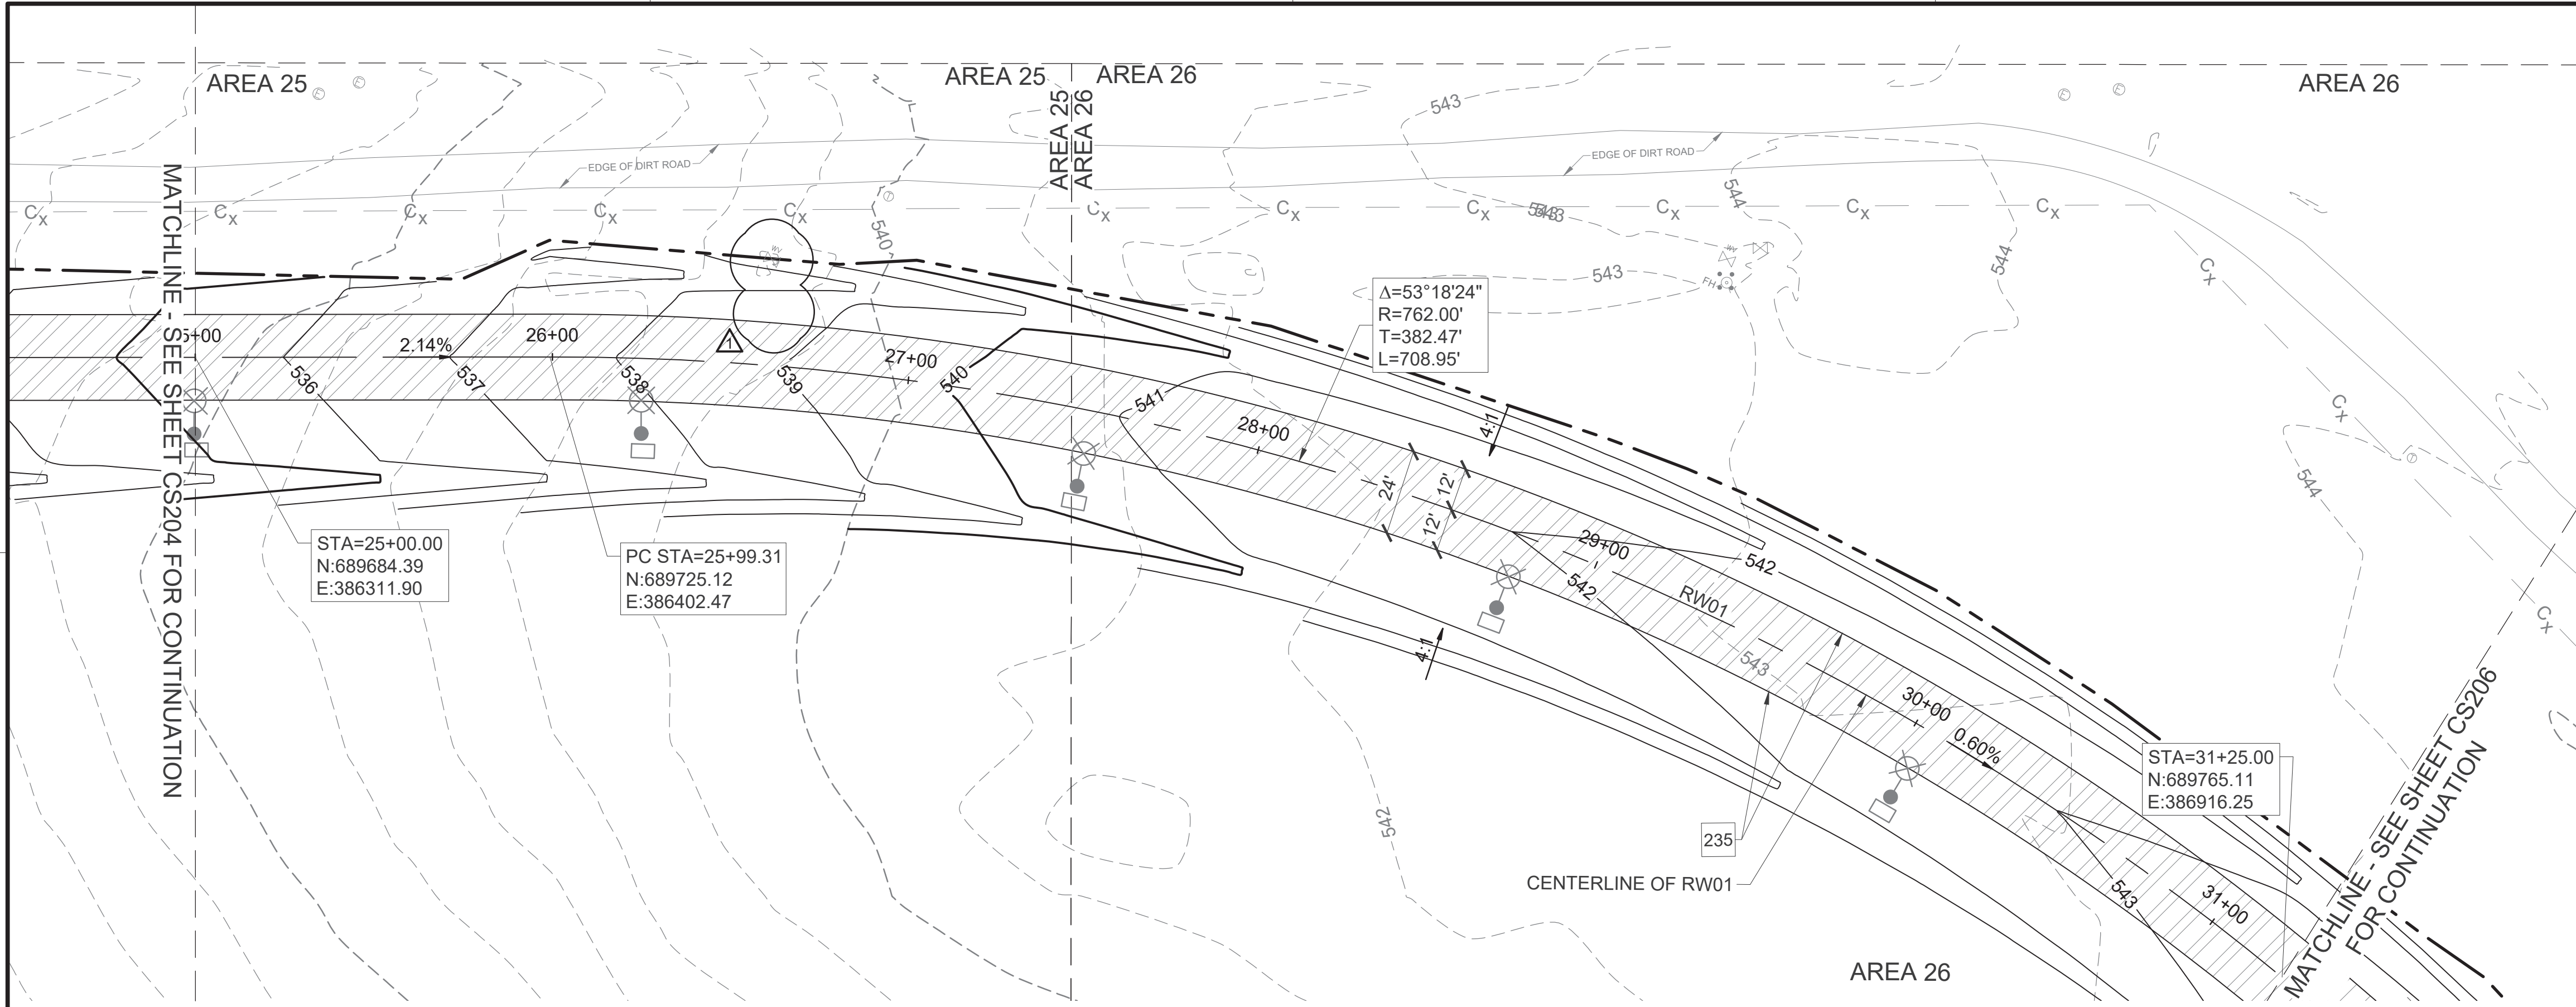

A1 ROADWAY PLAN & PROFILE RW01 STA 25+00-31+25 - AREA 25 & 26
SCALE: HORIZONTAL 1" = 30'
VERTICAL 1" = 5'

GENERAL NOTES

A REFER TO SHEETS CS503 AND CS504 FOR MARKING DETAILS



KEYNOTES

235 EDGE OF PAVEMENT / ASPHALT TAPER, RE: D4/CS501

LEGEND

- ASPHALT ROADWAY, RE: C3/CS501
- LIMITS OF DISTURBANCE
- EXISTING MAJOR CONTOUR
- EXISTING MINOR CONTOUR
- EXISTING UNDERGROUND COMM.
- MINOR CONTOUR
- MAJOR CONTOUR
- ROADWAY CENTERLINE
- STREET LIGHT POLE, RE: A3/ES503
- EXISTING COMMUNICATION MANHOLE
- EXISTING ELECTRICAL MANHOLE/HANDHOLE
- ELECTRICAL PULL BOX
- POINT OF CURVATURE

KEY PLAN

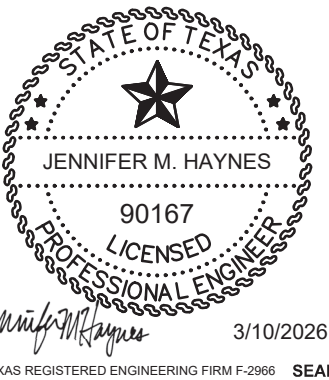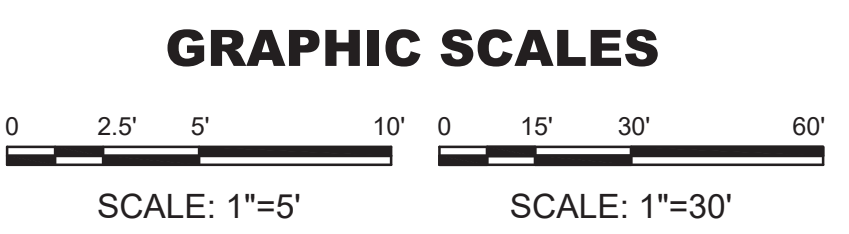

Jacobs **BURNS & MCDONNELL**
JACOBSRAM A JOINT VENTURE
1100 NORTH GLEBE ROAD
SUITE 500
ARLINGTON, VA 22201


APPROVED
FOR COMMANDER NAVFAC DATE 04/10/2026

ACTIVITY
AFMISC APPROVAL PER NAVFAC
SAT-TO CHECKLIST
SATISFACTORY TO DATE 31 DEC 2026
DES: JMH DRW: SMC REV: ATM
PM/DM KKK
BRANCH MANAGER SMK
CHIEF ENGINEER SMK
FIRE PROTECTION RO

DEPARTMENT OF THE NAVY
NAVAL FACILITIES ENGINEERING SYSTEMS COMMAND
NAVAL FACILITIES ENGINEERING SYSTEMS COMMAND - PACIFIC
NAVFAC PACIFIC
JOINT REGION MARIANAS (JRM)
ANDERSEN AIR FORCE BASE
GUAM
FY24 AJJY183012 (P-012),
PDI: NORTH AIRCRAFT PARKING RAMP
ROADWAY PLAN & PROFILE RW01 STA 25+00-31+25 - AREA 25 & 26

SCALE: AS SHOWN
PROJECTS NO.: 1665555
CONSTR CONTROL NO.
NAVFAC DRAWING NO. 17361759
SHEET 136 OF 377
CS205

FILE NAME: U:\BLOG\NAVFAC Pacific\03430603 - P-012 North Aircraft Parking Ramp\700 Working Documents\740.01 Civil\012_1665555_CG124.dwg
LAYOUT NAME: GRADING AND DRAINAGE PLAN - AREA 23
PLOTTED: 03/09/2026 2:07pm
USER: CameroS

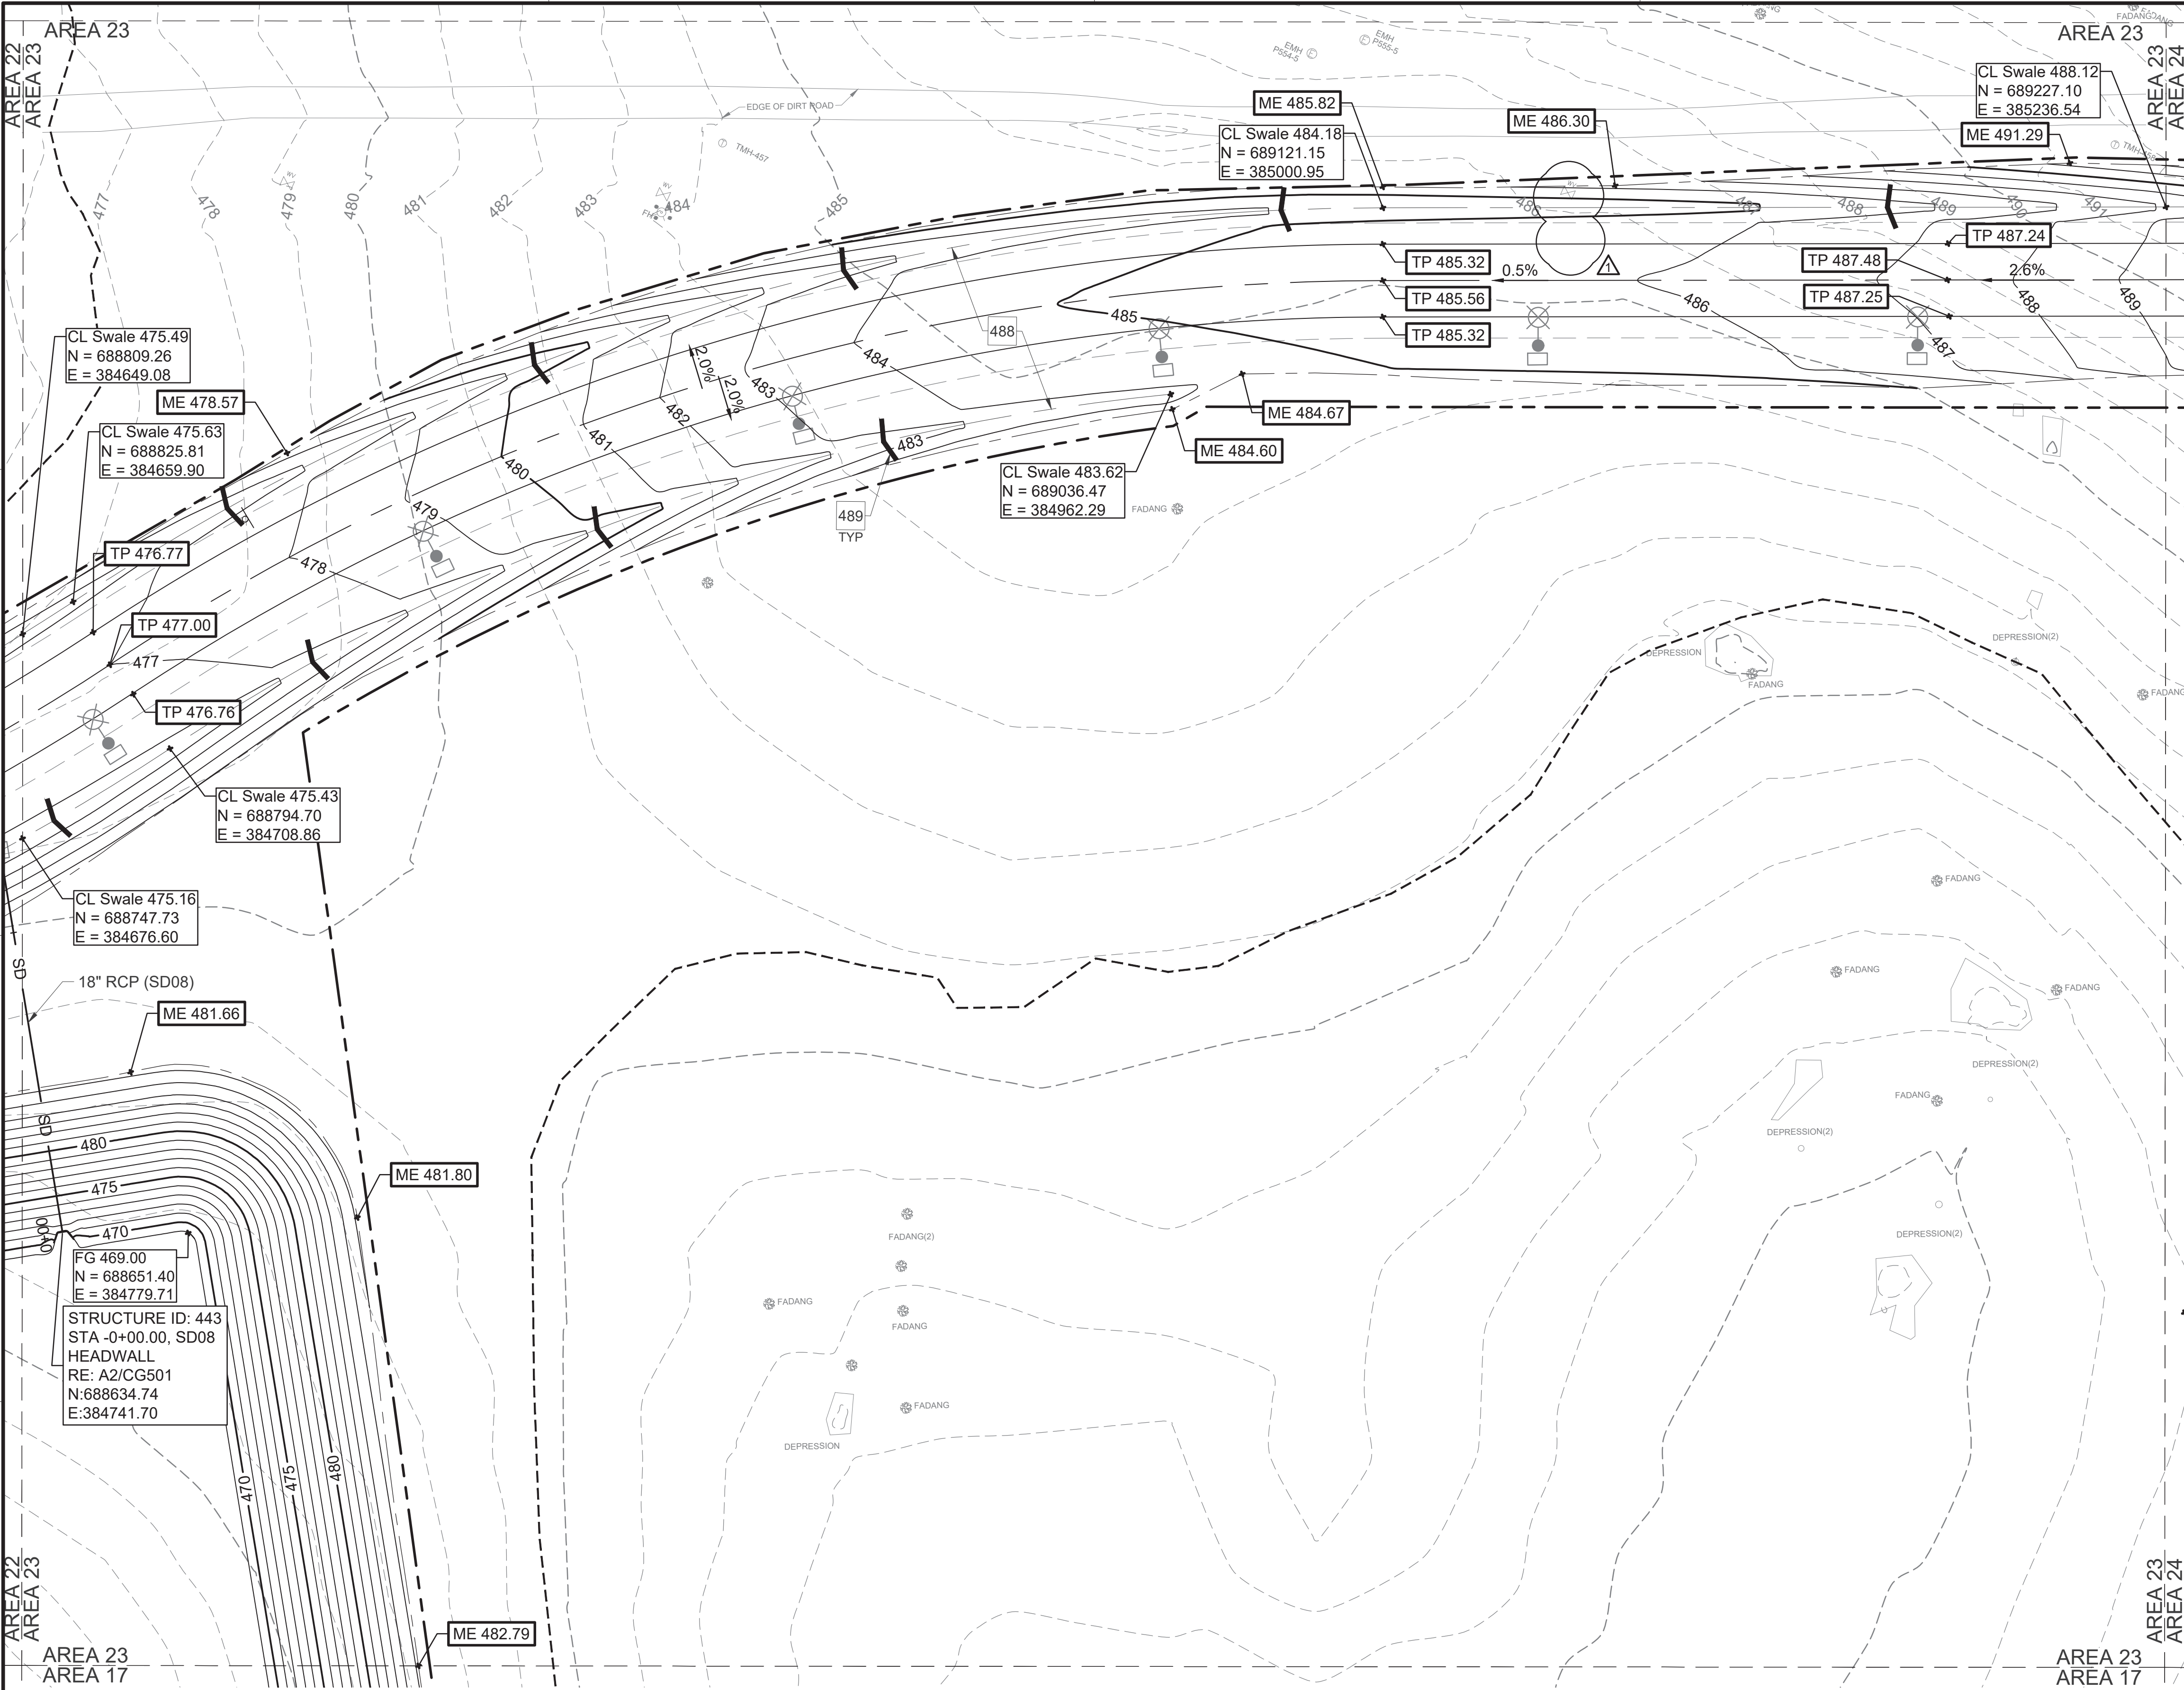


GENERAL NOTES	
A	CONTOURS ARE AT 1' INTERVALS
B	ADJUST NEW AND EXISTING UTILITY COVERS TO NEW GRADE
C	REFER TO SHEETS CS201 TO CS207 FOR ROADWAY PROFILES
D	REFER TO SHEETS CG201 TO CG210 FOR STORM DRAIN PROFILES
E	EXCAVATED SOIL WILL BE STOCKPILED ON SITE IN THE NORTHEAST CORNER AND NORTHWEST CORNER OF THE SITE. REFER TO SHEET GI001 FOR RECOMMENDED STOCKPILE AREAS.

KEYNOTES	
488	2.0' BOTTOM DRY SWALE, RE: D1/CG502
489	ROCK CHECK DAM, RE: C3/CG503



LEGEND	
---	LIMITS OF DISTURBANCE
---	LIMITS OF GRADING
---	EXISTING SINKHOLE
---	EXISTING MAJOR CONTOUR
---	EXISTING MINOR CONTOUR
---	MINOR CONTOUR
---	MAJOR CONTOUR
---	CENTERLINE OF SWALE
---	ROADWAY CENERLINE
---	TOP & BOTTOM OF BASIN
SD	STORM DRAIN
---	HEADWALL, RE: A2/CG501
TP	TOP OF PAVEMENT ELEVATION
FG	FINISHED GRADE ELEVATION
ME	MATCH EXISTING ELEVATION
CL	CENTERLINE ELEVATION
XXX	SLOPE (PERCENT)

---	EXISTING WATER VALVE
---	EXISTING COMMUNICATION MANHOLE
---	EXISTING ELECTRICAL MANHOLE

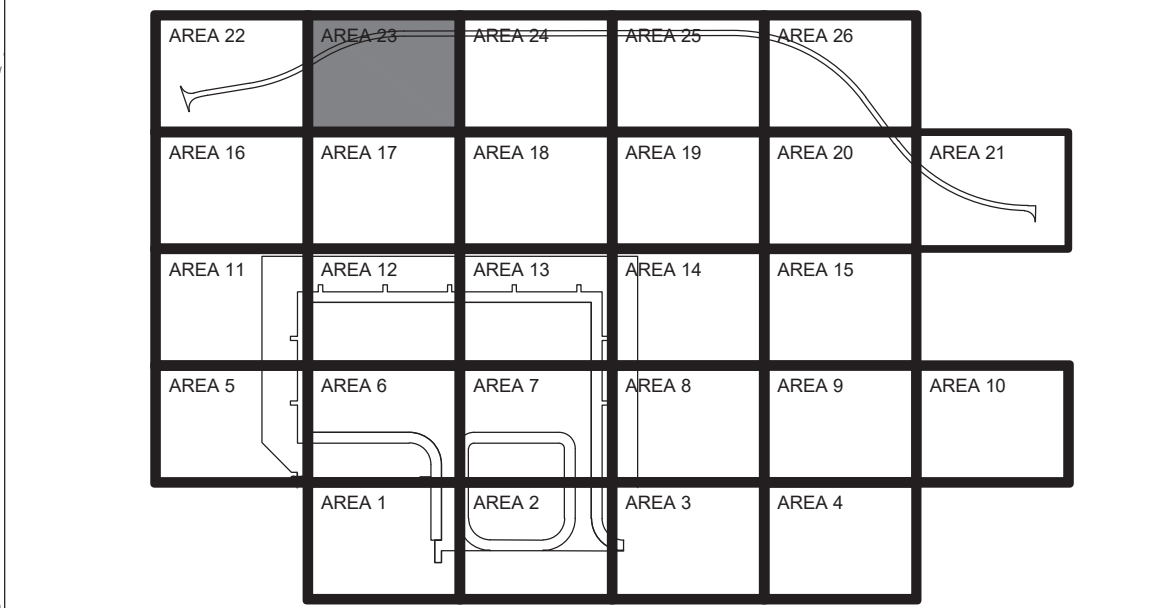

AREA 23 KEY PLAN	
GRAPHIC SCALE	
SCALE: 1"=30'	
NORTH ARROW	

REVISIONS	
1	AMEND 002 - REVISED FHS
DATE	03-MAR-26

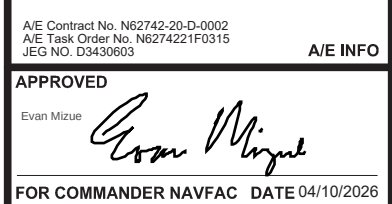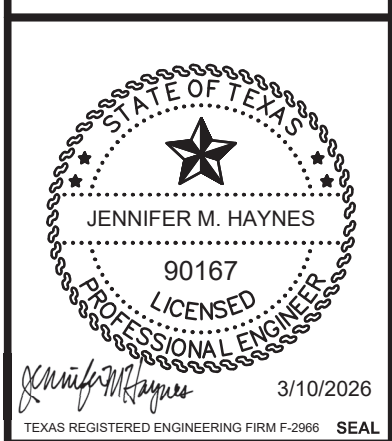

ACTIVITY		
AFIMSC APPROVAL PER NAVFAC SAT-TO CHECKLIST		
SATISFACTORY TO DATE		
31 DEC 2025		
DES: JMH	DRW: SMC	REV: ATM
PM/DM		KKK
BRANCH MANAGER		SMK
CHIEF ENG/ARCH		SMK
FIRE PROTECTION		RO

DEPARTMENT OF THE NAVY	NAVAL FACILITIES ENGINEERING SYSTEMS COMMAND	GUAM
NAVFAC PACIFIC	NAVAL FACILITIES ENGINEERING SYSTEMS COMMAND - PACIFIC	
ANDERSEN AIR FORCE BASE	JOINT REGION MARIANAS (JRM)	
FY24 AJY183012 (P-012)		
PDI: NORTH AIRCRAFT PARKING RAMP		
GRADING AND DRAINAGE PLAN - AREA 23		

SCALE:	AS SHOWN
EPROJECTS NO.:	1665555
CONSTR CONTROL NO.	
NAVFAC DRAWING NO.	17361821
SHEET	199 OF 377
CG124	

IF SHEET IS LESS THAN 22" X 34"
REDUCED PRINT. USE GRAPHIC SCALES



A	CONTOURS ARE AT 1' INTERVALS
B	ADJUST NEW AND EXISTING UTILITY COVERS TO NEW GRADE
C	REFER TO SHEETS CS201 TO CS207 FOR ROADWAY PROFILES
D	EXCAVATED SOIL WILL BE STOCKPILED ON SITE IN THE NORTHEAST CORNER AND NORTHWEST CORNER OF THE SITE. REFER TO SHEET G1001 FOR RECOMMENDED STOCKPILE AREAS.


——— ———	LIMITS OF DISTURBANCE
——— ———	LIMITS OF GRADING
-----525-----	EXISTING MAJOR CONTOUR
-----524-----	EXISTING MINOR CONTOUR
———524———	MINOR CONTOUR
———525———	MAJOR CONTOUR
——— ———	ROADWAY CENTERLINE
TP	TOP OF PAVEMENT ELEVATION
ME	MATCH EXISTING ELEVATION

The diagram shows a road cross-section with a wavy line representing the ground surface. Above the surface, a horizontal line with an arrow pointing right is labeled 'XXX' and 'SLOPE (PERCENT)'. Below the surface, there are three symbols: a triangle with a cross inside, a circle with a cross inside, and a circle with a dot inside. To the right of the road, there is a triangle with an exclamation mark inside.


△	EXISTING WATER VALVE
⊗	EXISTING ELECTRICAL MANHOLE/HANDHOLE
⊙	EXISTING COMMUNICATION MANHOLE



SCALE: 1"=30'

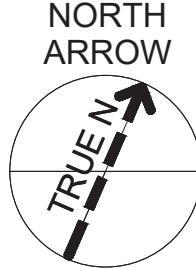REDESIGN FINAL SUBMITTAL

FILE NAME: U:\BLOG\NAVFAC Pacific\03430603 - P-012 North Aircraft Parking Ramp\700 Working Documents\740 Sheets\740.01_Civil\0102_1665555_CG144.dwg
LAYOUT NAME: KARST FEATURES PLAN
PLOTTED: 03/10/2026 4:31pm
USER: CameroS

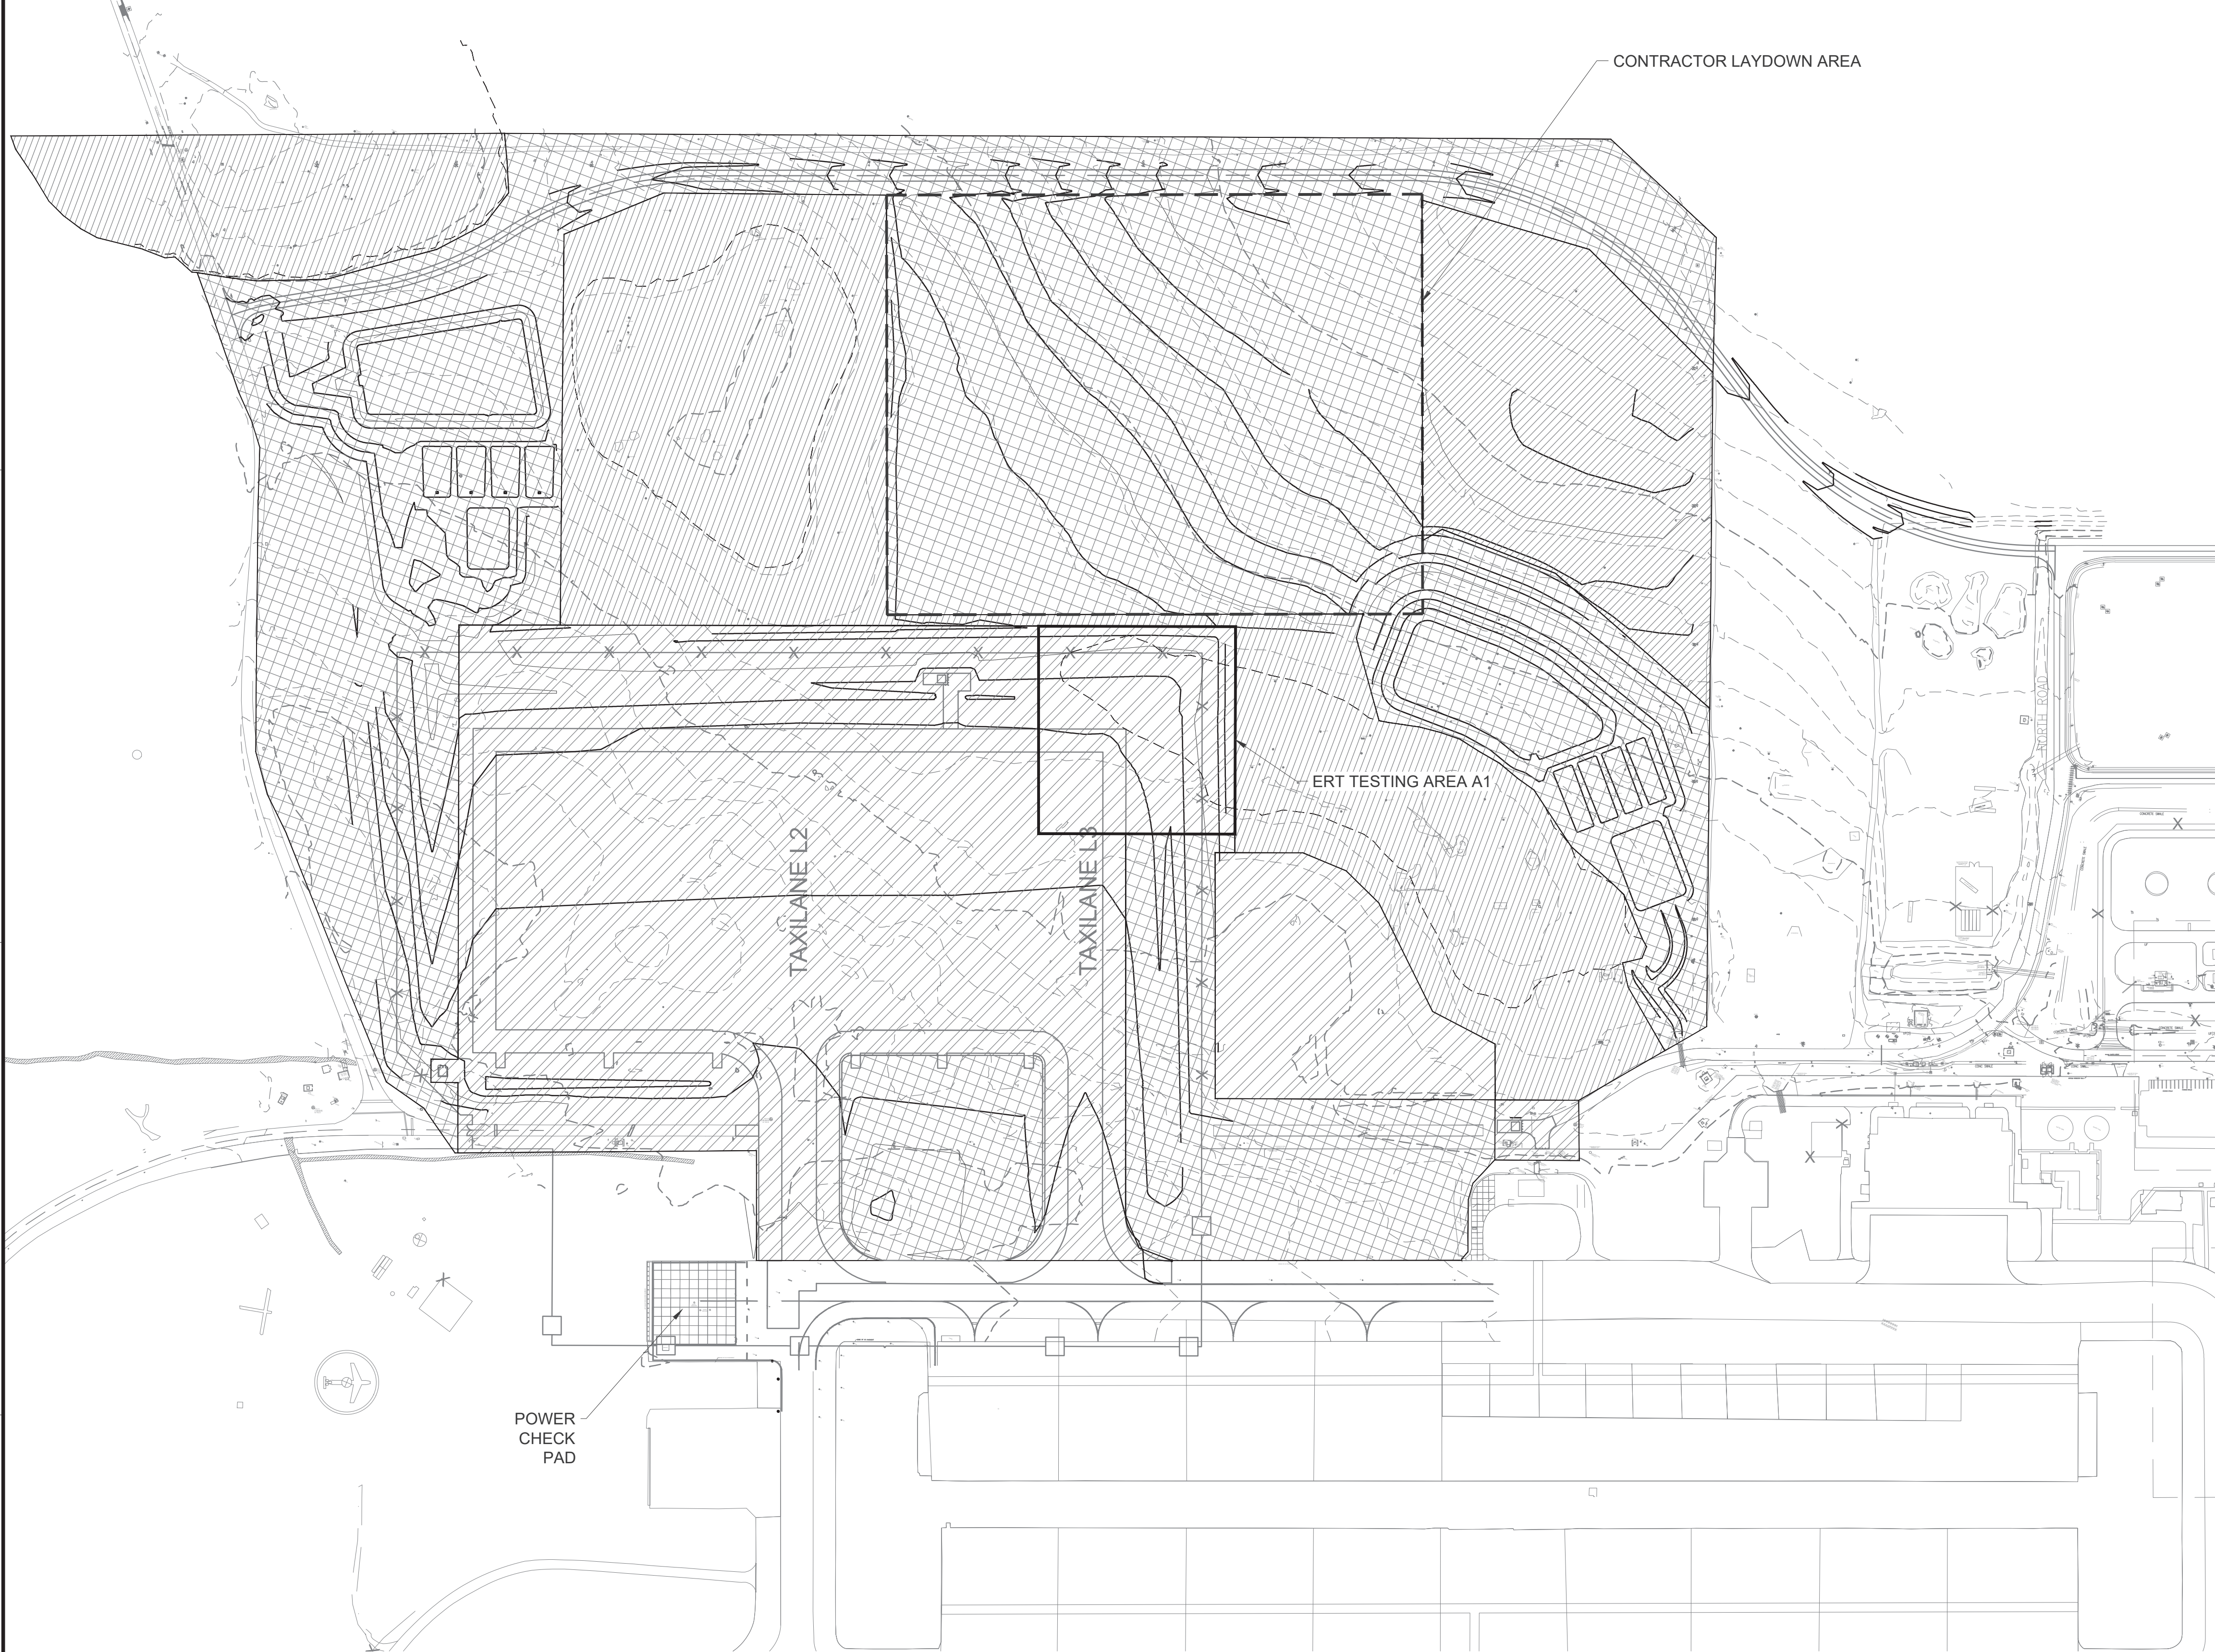

- ### GENERAL NOTES
- A HIRE FULL-TIME HYDRO GEOLOGIST (WITH GUAM EPA APPROVED CREDENTIALS), WHO MUST BE PRESENT WHEN EARTHWORK IS BEING PERFORMED.
 - B HIRE FULL-TIME GEOTECHNICAL ENGINEER WITH EXPERIENCE IN THE MARIANAS ISLANDS OR HAWAII, WHO MUST BE PRESENT WHEN EARTHWORK IS BEING PERFORMED.
 - C FOR AREAS RECEIVING GROUT AS SHOWN ON CG146, STOP GROUTING AT 10CY PER HOLE/PIPE SHAFT/SOLUTION TUBE AND CONTACT THE CONTRACTING OFFICER IF 10CY DID NOT RESULT IN VISIBLE FILLING OF VOID.
 - D FOR AREAS RECEIVING GROUT AS SHOWN ON CG146, TOP OFF VOID AFTER 10CY HAS BEEN PLACED DUE TO SETTLING OR IF GROUT DID NOT REACH ADJACENT GROUND SURFACE ELEVATION.
 - E SEE KARST FEATURES DETAIL ON CG146 FOR SINKHOLE REPAIR REQUIREMENTS.
 - F IF KARST FEATURES ARE FOUND IN THE CONTRACTOR LAYDOWN AREA OR PFAS RELOCATION AREA, NOTIFY THE CONTRACTING OFFICER.


LEGEND

- Zone 1 - GROUTED SURFACE FEATURES (IMPERMEABLE INFILL)
- Zone 2 - BOULDER/GRAVEL FEATURES (PERMEABLE INFILL)
- Zone 3 - UNMITIGATED AREA
- PERIMETER OF MAPPED EXISTING SINKHOLE

ID	AREA (ACRE)	MIN. NO. OF ERT LINES	MIN. TOTAL LENGTH OF ERT TESTING (FT)
A1	4.4	10*	5,000*
---	---	---	37,000**

* MINIMUM VALUES INCLUDE EXTENDING ERT TESTING 100-FT BEYOND THE MAPPED EXTENTS OF EXISTING SINKHOLES SHOWN ON THE DRAWINGS, IN ACCORDANCE WITH SPECIFICATION 31 00 00, SUBSECTION 3.3.3, ELECTRICAL RESISTIVITY TOMOGRAPHY (ERT).

** MINIMUM VALUE INDICATES ADDITIONAL ERT TESTING TO BE PERFORMED AT UNMAPPED SINKHOLES AS APPROVED BY THE CONTRACTING OFFICER, AND IN ACCORDANCE WITH SPECIFICATION 31 00 00, SUBSECTION 3.3.3, ELECTRICAL RESISTIVITY TOMOGRAPHY (ERT).

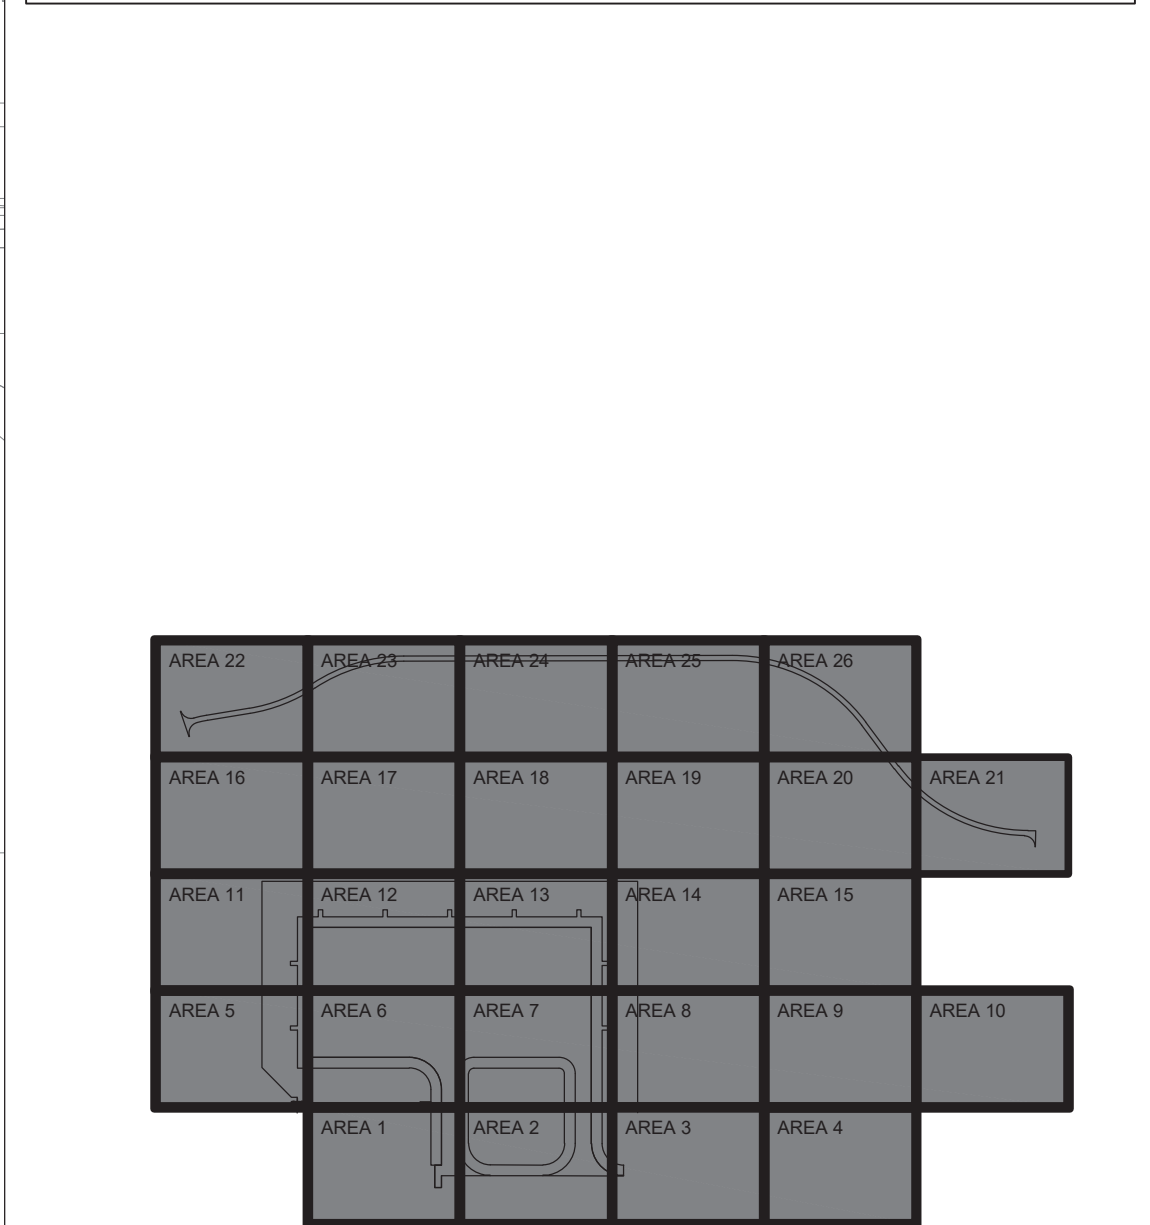

OVERALL KEY PLAN

GRAPHIC SCALE


0 100' 200' 400'

SCALE: 1"=200'

NORTH ARROW

TRUE N

SYMBOL	DESCRIPTION	DATE
1	AMEND 0002 - REVISED LEGEND	10MAR26

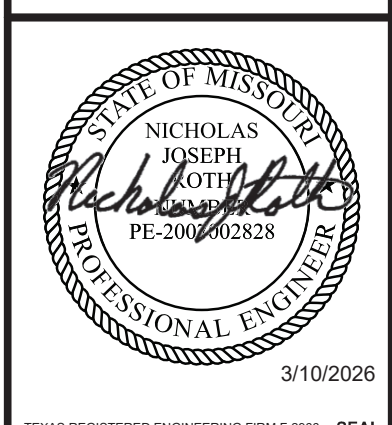

APPROVED

FOR COMMANDER NAVFAC DATE 04/10/2026

ACTIVITY

AFMISC APPROVAL PER NAVFAC SAT-TO CHECKLIST

SATISFACTORY TO DATE 31 DEC 2026

DES: JMH DRW: SMC REV: ATM

PMIDM KKK

BRANCH MANAGER SMK

CHIEF ENGINEER SMK

FIRE PROTECTION RO

DEPARTMENT OF THE NAVY
NAVFAC PACIFIC
ANDERSEN AIR FORCE BASE

NAVAL FACILITIES ENGINEERING SYSTEMS COMMAND
NAVAL FACILITIES ENGINEERING SYSTEMS COMMAND - PACIFIC
JOINT REGION MARIANAS (JRM)

GUAM

FY24 AUJY183012 (P-012)
PDI: NORTH AIRCRAFT PARKING RAMP
KARST FEATURES PLAN

SCALE: AS SHOWN

EPROJECTS NO.: 1665555

CONSTR CONTROL NO.

NAVFAC DRAWING NO. 17361839

SHEET 216 OF 377


CG144

IF SHEET IS LESS THAN 22" X 34"
REDUCED PRINT. USE GRAPHIC SCALES

REDESIGN FINAL SUBMITTAL



FILE NAME: \\FTWFL13\Projects\DFW\Bldg\NAVFAC Pacific\0340603 - P-012 North Aircraft Parking Ramp\700 Working Documents\740 Sheets\740.01 Civil\012_1665555_CG146.dwg
LAYOUT NAME: KARST FEATURES DETAIL
PLOTTED: 04/08/2026 6:02pm
USER: MerdesFX

A1 KARST FEATURES DETAIL
SCALE: N.T.S.

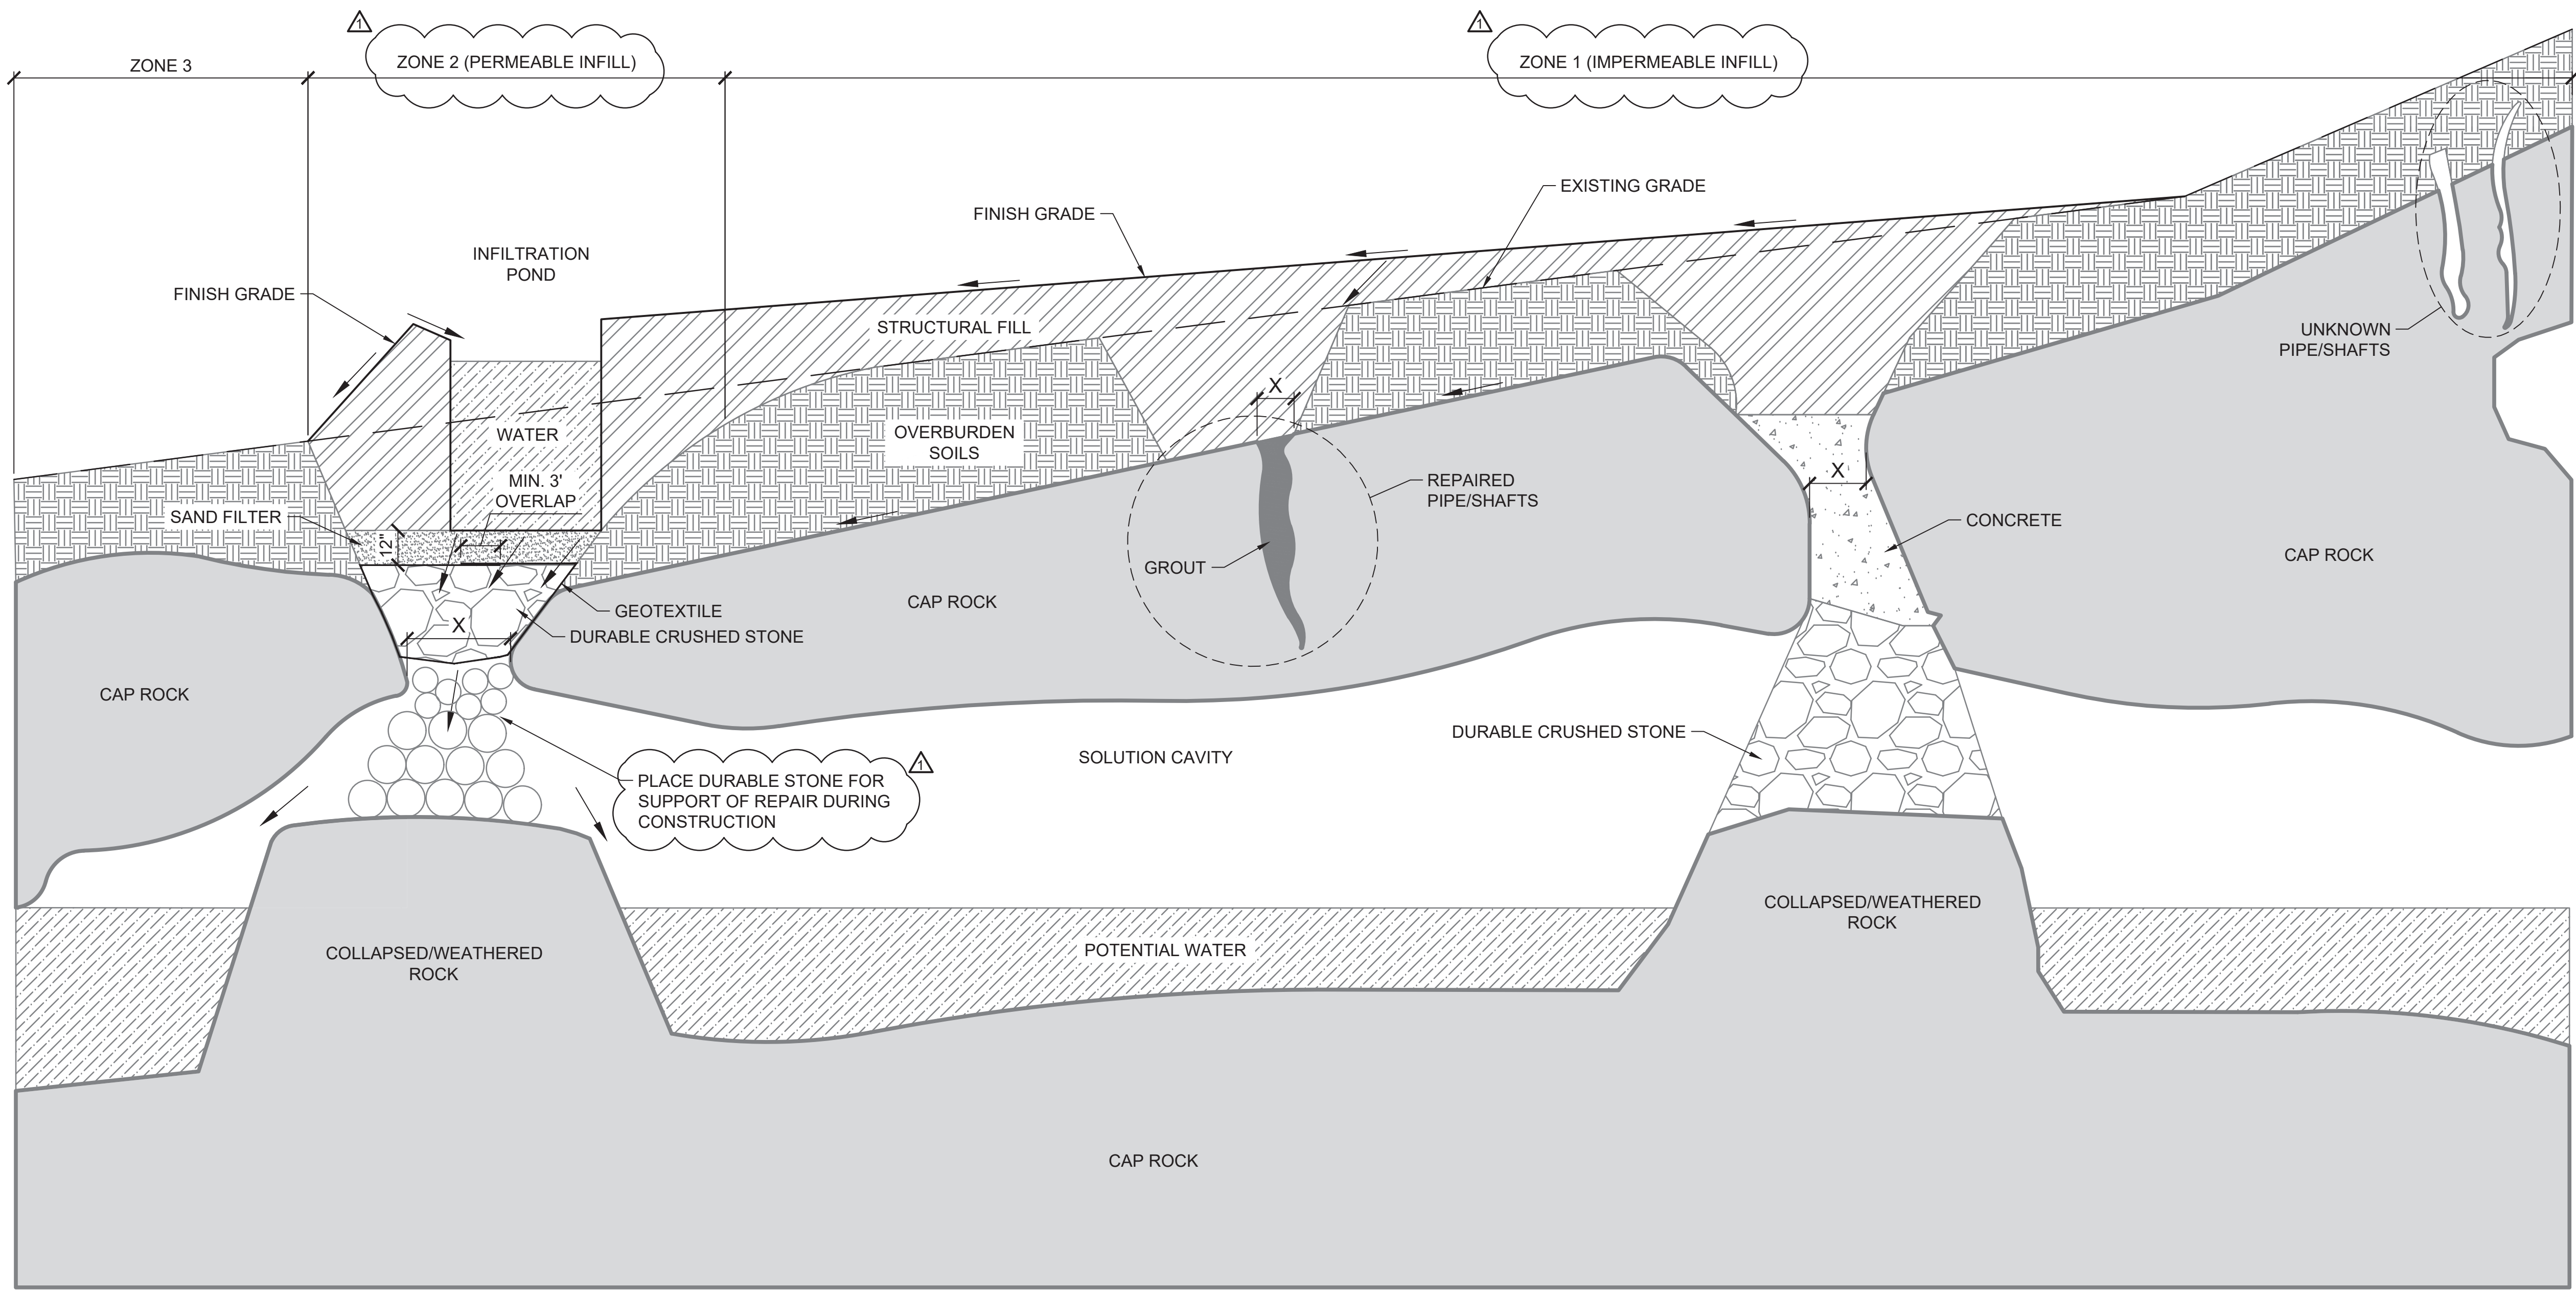

- X WIDTH OF SINKHOLE "THROAT".
- <1 FT
1 TO < 3 FT
3 TO 6 FT
> 6 FT
- PLACE GROUT (SAND-CEMENT) MIXTURE INTO OPEN CAVITY.
- ZONE 1: PLACE CRUSHED STONE WITH A MINIMUM PARTICLE DIAMETER OF 18 INCHES UP TO THE THROAT OF THE SINKHOLE. CAP WITH LOW SLUMP (4-IN), STRUCTURAL GRADE CONCRETE A MINIMUM OF 3 FEET ABOVE THE THROAT OR THE GROUND SURFACE; WHICHEVER IS LOWER. STONE MUST BE A DURABLE MATERIAL.
- ZONE 2: PLACE STONE WITH PARTICLE SIZES RANGING FROM 4 TO 12 INCHES UP TO THE BASE OF THE THROAT OF THE SINKHOLE FOR SUPPORT. A GEOTEXTILE MUST THEN BE PLACED TO LINE THE HOLE. PLACE CRUSHED STONE WITH A MINIMUM PARTICLE DIAMETER OF 18 INCHES OVER GEOTEXTILE, AND FULLY ENCAPSULATED THE CRUSHED STONE BY WRAPPING IT IN GEOTEXTILE. STONE MUST BE A DURABLE MATERIAL. ABOVE THE GEOTEXTILE-ENCAPSULATED CRUSHED STONE LAYER, PLACE A 12-INCH THICK SAND FILTER IN ACCORDANCE WITH SPECIFICATION SECTION 31 00 00 "EARTHWORK".
- ZONE 1: PLACE DURABLE CRUSHED STONE RANGING FROM 24 TO 36 INCHES UP TO THE THROAT OF THE SINKHOLE. CAP WITH LOW SLUMP (4-IN), STRUCTURAL GRADE CONCRETE A MINIMUM OF 4 FEET ABOVE THE THROAT OR THE GROUND SURFACE; WHICHEVER IS LOWER. CLEAN STONE, DEFINED AS A DURABLE STONE WITH 6 PERCENT FINES OR LESS AT THE TIME OF PLACEMENT, WITH DIAMETERS RANGING FROM 6 TO 18 INCHES CAN BE PLACED IN WET CONCRETE TO REDUCE THE REQUIRED VOLUME OF CONCRETE TO FACILITATE THE CONSTRUCTION OF IMPERMEABLE STRUCTURAL CONCRETE CAP.
- ZONE 2: PLACE STONE WITH PARTICLE SIZES RANGING FROM 8 TO 16 INCHES UP TO THE BASE OF THE THROAT OF THE SINKHOLE FOR SUPPORT. A GEOTEXTILE MUST THEN BE PLACED TO LINE THE HOLE. PLACE CRUSHED STONE WITH A MINIMUM PARTICLE DIAMETER OF 24 INCHES OVER GEOTEXTILE, AND FULLY ENCAPSULATED THE CRUSHED STONE BY WRAPPING IT IN GEOTEXTILE. STONE MUST BE A DURABLE MATERIAL. ABOVE THE GEOTEXTILE-ENCAPSULATED CRUSHED STONE LAYER, PLACE A 12-INCH THICK SAND FILTER IN ACCORDANCE WITH SPECIFICATION SECTION 31 00 00 "EARTHWORK".
- THE CONTRACTOR'S HYDROGEOLOGIST/GEOTECHNICAL ENGINEER MUST SUBMIT A KARST REPAIR METHODOLOGY TO THE CONTRACTING OFFICER ENTITLED "KARST FEATURE REPAIR METHODOLOGY AND HYDROGEOLOGIC ASSESSMENT REPORT". THE METHODOLOGY MUST BE BASED ON AND INDICATE THE REPAIR TYPE ZONE SHOWN ON CG144 AND CG145 THAT IS REQUIRED TO GUARANTEE THE PROJECT'S DESIGN. THE METHODOLOGY MUST ALSO INCLUDE THE ERT DATA REPORT ENTITLED "SUBSURFACE EXTENTS OF KARST FEATURES REPORT" DELINEATING THE SUBSURFACE EXTENTS OF THE FEATURE, AND THE DIMENSIONS AND THE LOCATION OF THE FEATURE AND OTHER REQUIREMENTS AS INDICATED IN SPECIFICATION SECTION 31 00 00 "EARTHWORK" PARAGRAPH 3.3.3. UPON REVIEW OF THE PROPOSED REPAIR METHODOLOGY BY THE CONTRACTING OFFICER, THE DOR AND GEPA, A REPAIR METHOD WILL BE ISSUED TO THE CONTRACTOR.

SYMBOL	DESCRIPTION	DATE
1	AMEND 0002 - REVISED ZONE LABELS	10-MAR-26

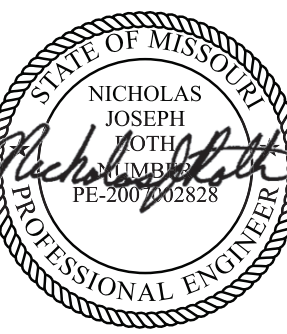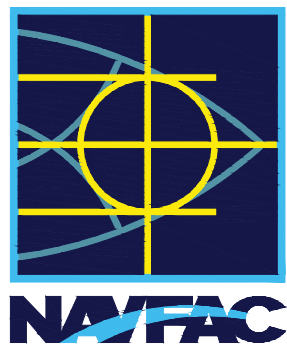

JACOBS BURNS & MCDONNELL
JACOBSRAM A JOINT VENTURE
1100 NORTH GLEBE ROAD
SUITE 500
ARLINGTON, VA 22201
A/E Contract No. 160742-20-0003
A/E Task Order No. 160742-20-0003
A/E No. 026890 160742-20-0003

APPROVED
DATE 04/10/2026
FOR COMMANDER NAVFAC

ACTIVITY
AFMISC APPROVAL PER NAVFAC
SAT-TO CHECKLIST

SATISFACTORY TO DATE 31 DEC 2026

DES: JMH DRW: SMC REV: ATM
PMIDM KKK
BRANCH MANAGER SMK
CHIEF ENGINEER SMK
FIRE PROTECTION RO

DEPARTMENT OF THE NAVY
NAVAL FACILITIES ENGINEERING SYSTEMS COMMAND
NAVAL FACILITIES ENGINEERING SYSTEMS COMMAND - PACIFIC
JOINT REGION MARIANAS (JRM)
NAVFAC PACIFIC
ANDERSEN AIR FORCE BASE
GUAM
FY24 AUJY183012 (P-012)
PDI: NORTH AIRCRAFT PARKING RAMP
KARST FEATURES DETAIL

SCALE: AS SHOWN
PROJECTS NO.: 1665555
CONSTR CONTROL NO.
NAVFAC DRAWING NO. 17361841
SHEET 219 OF 377
CG146


FILE NAME: U:\BLDG NAVFAC Pacific\03430603 - P-012 North Aircraft Parking Ramp\700 Working Documents\740 Sheets\740.01 Civil\012_1665555_CG203.dwg
PLOTED: 03/09/2026 12:26pm
USER: CameroS

D


C

B

A

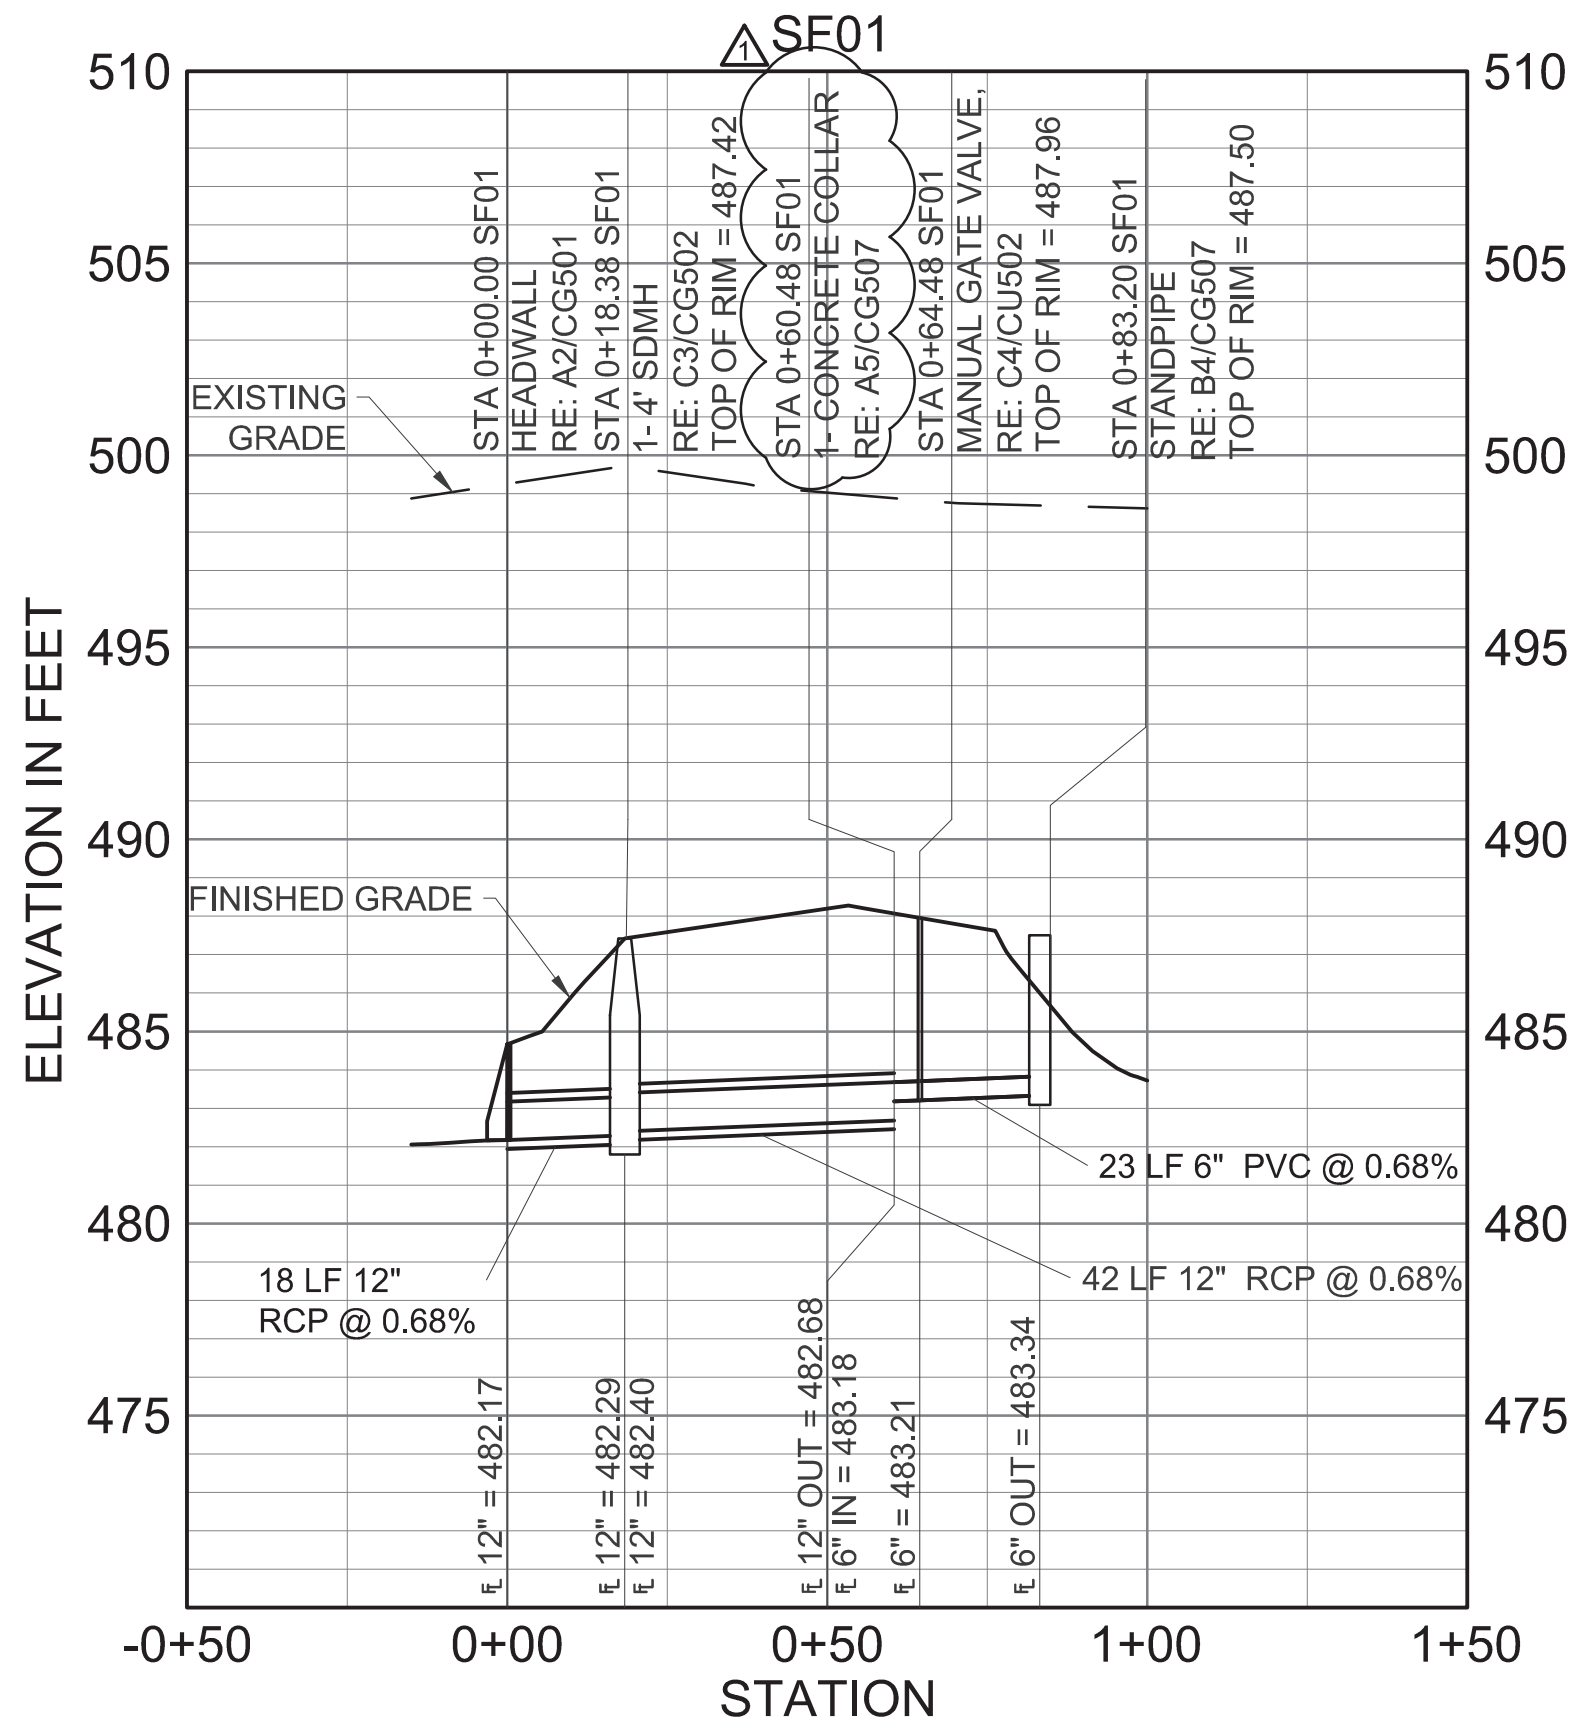


C1 DRAINAGE PROFILES - SF01
SCALE: HORIZONTAL 1" = 30'
VERTICAL 1" = 5'

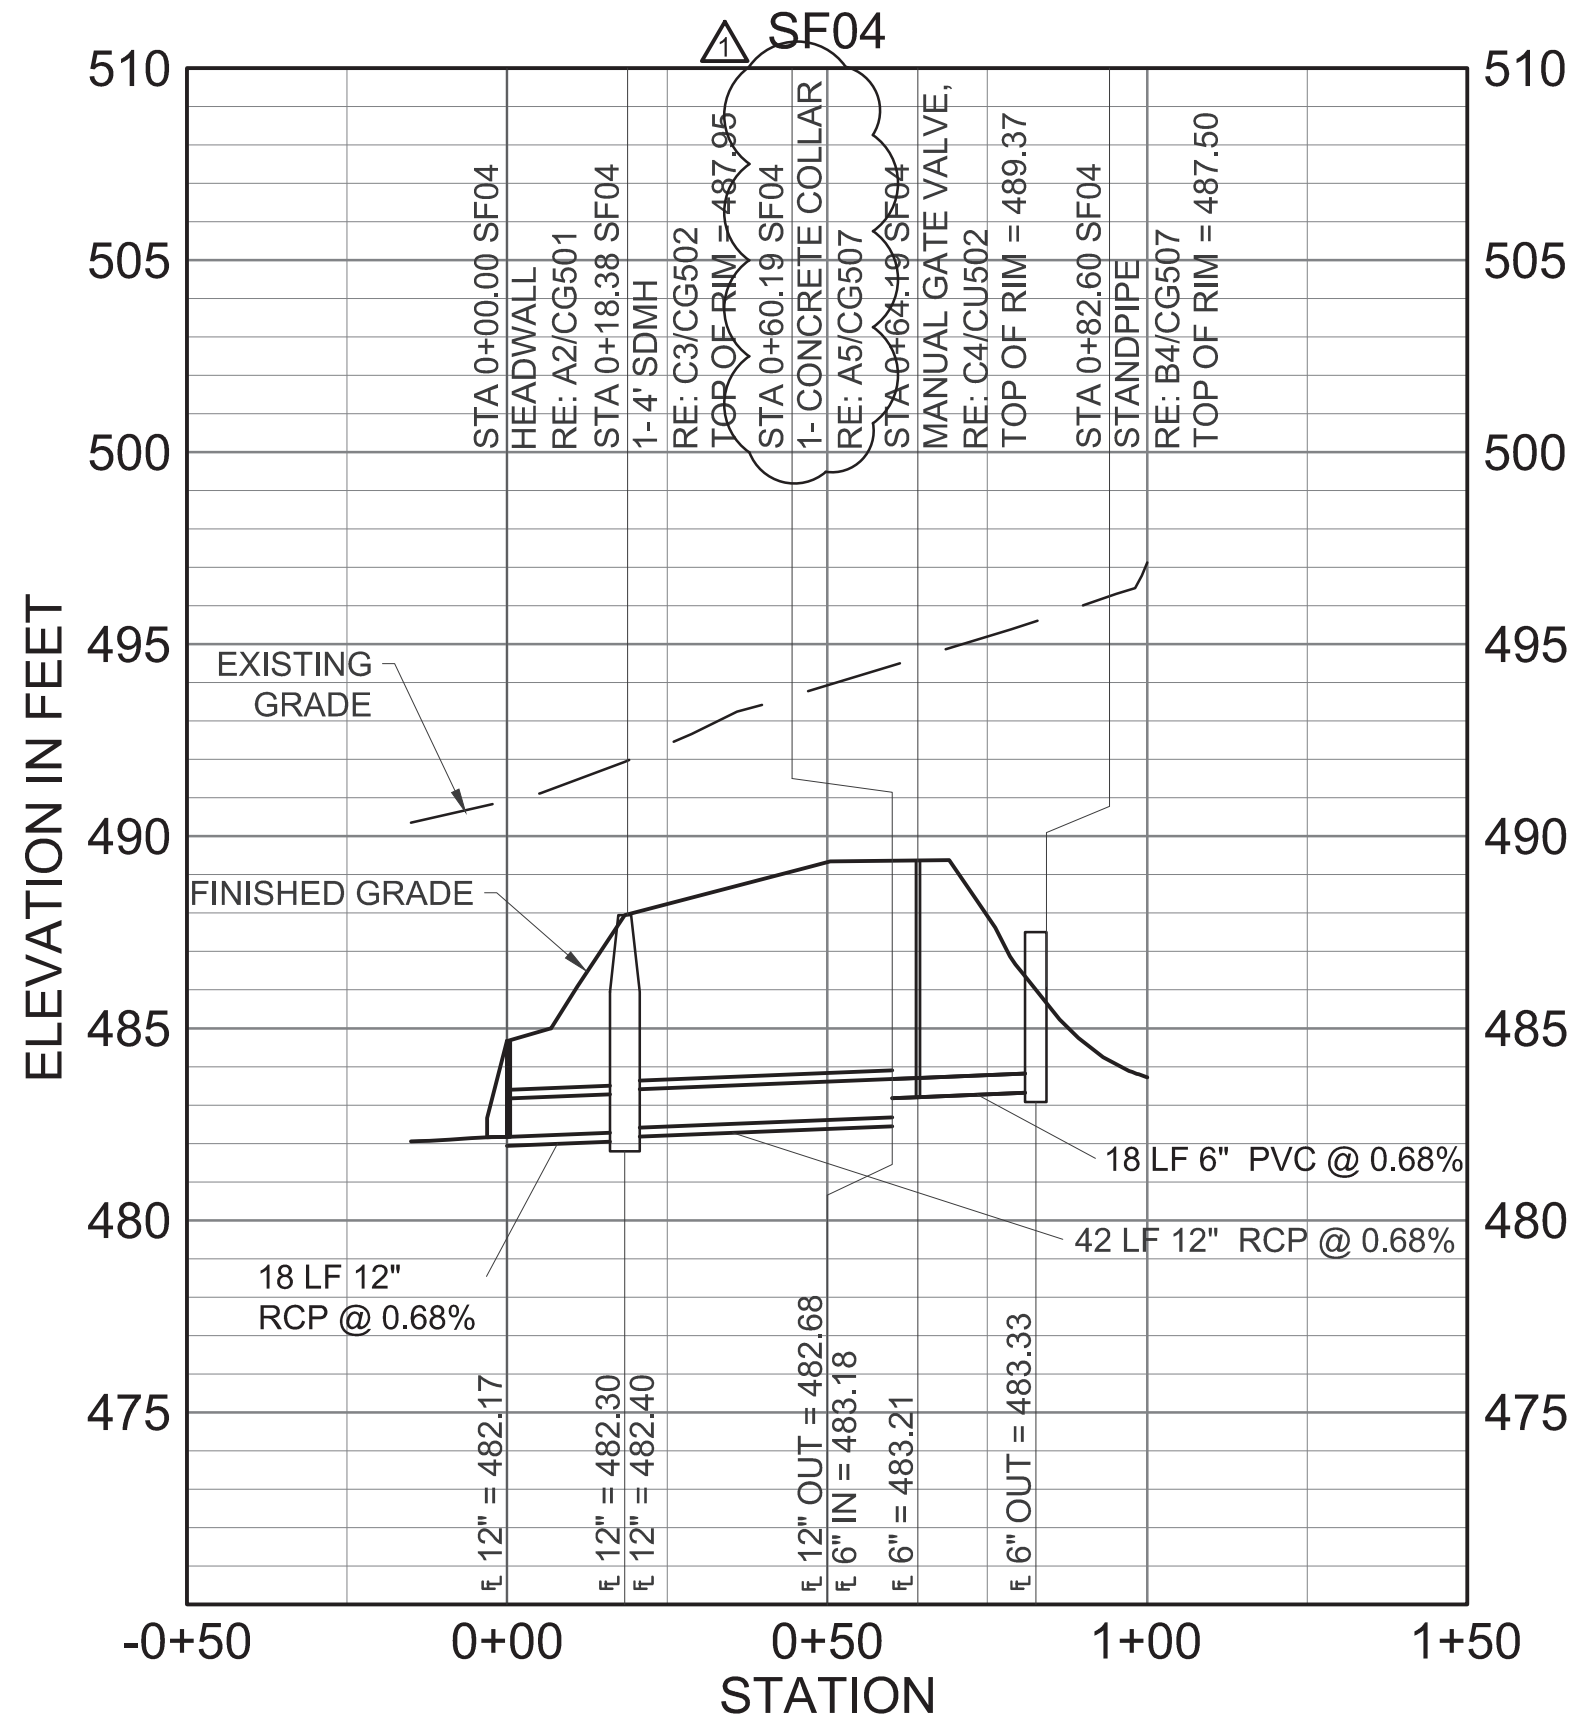


A1 DRAINAGE PROFILES - SF04
SCALE: HORIZONTAL 1" = 30'
VERTICAL 1" = 5'

2

2

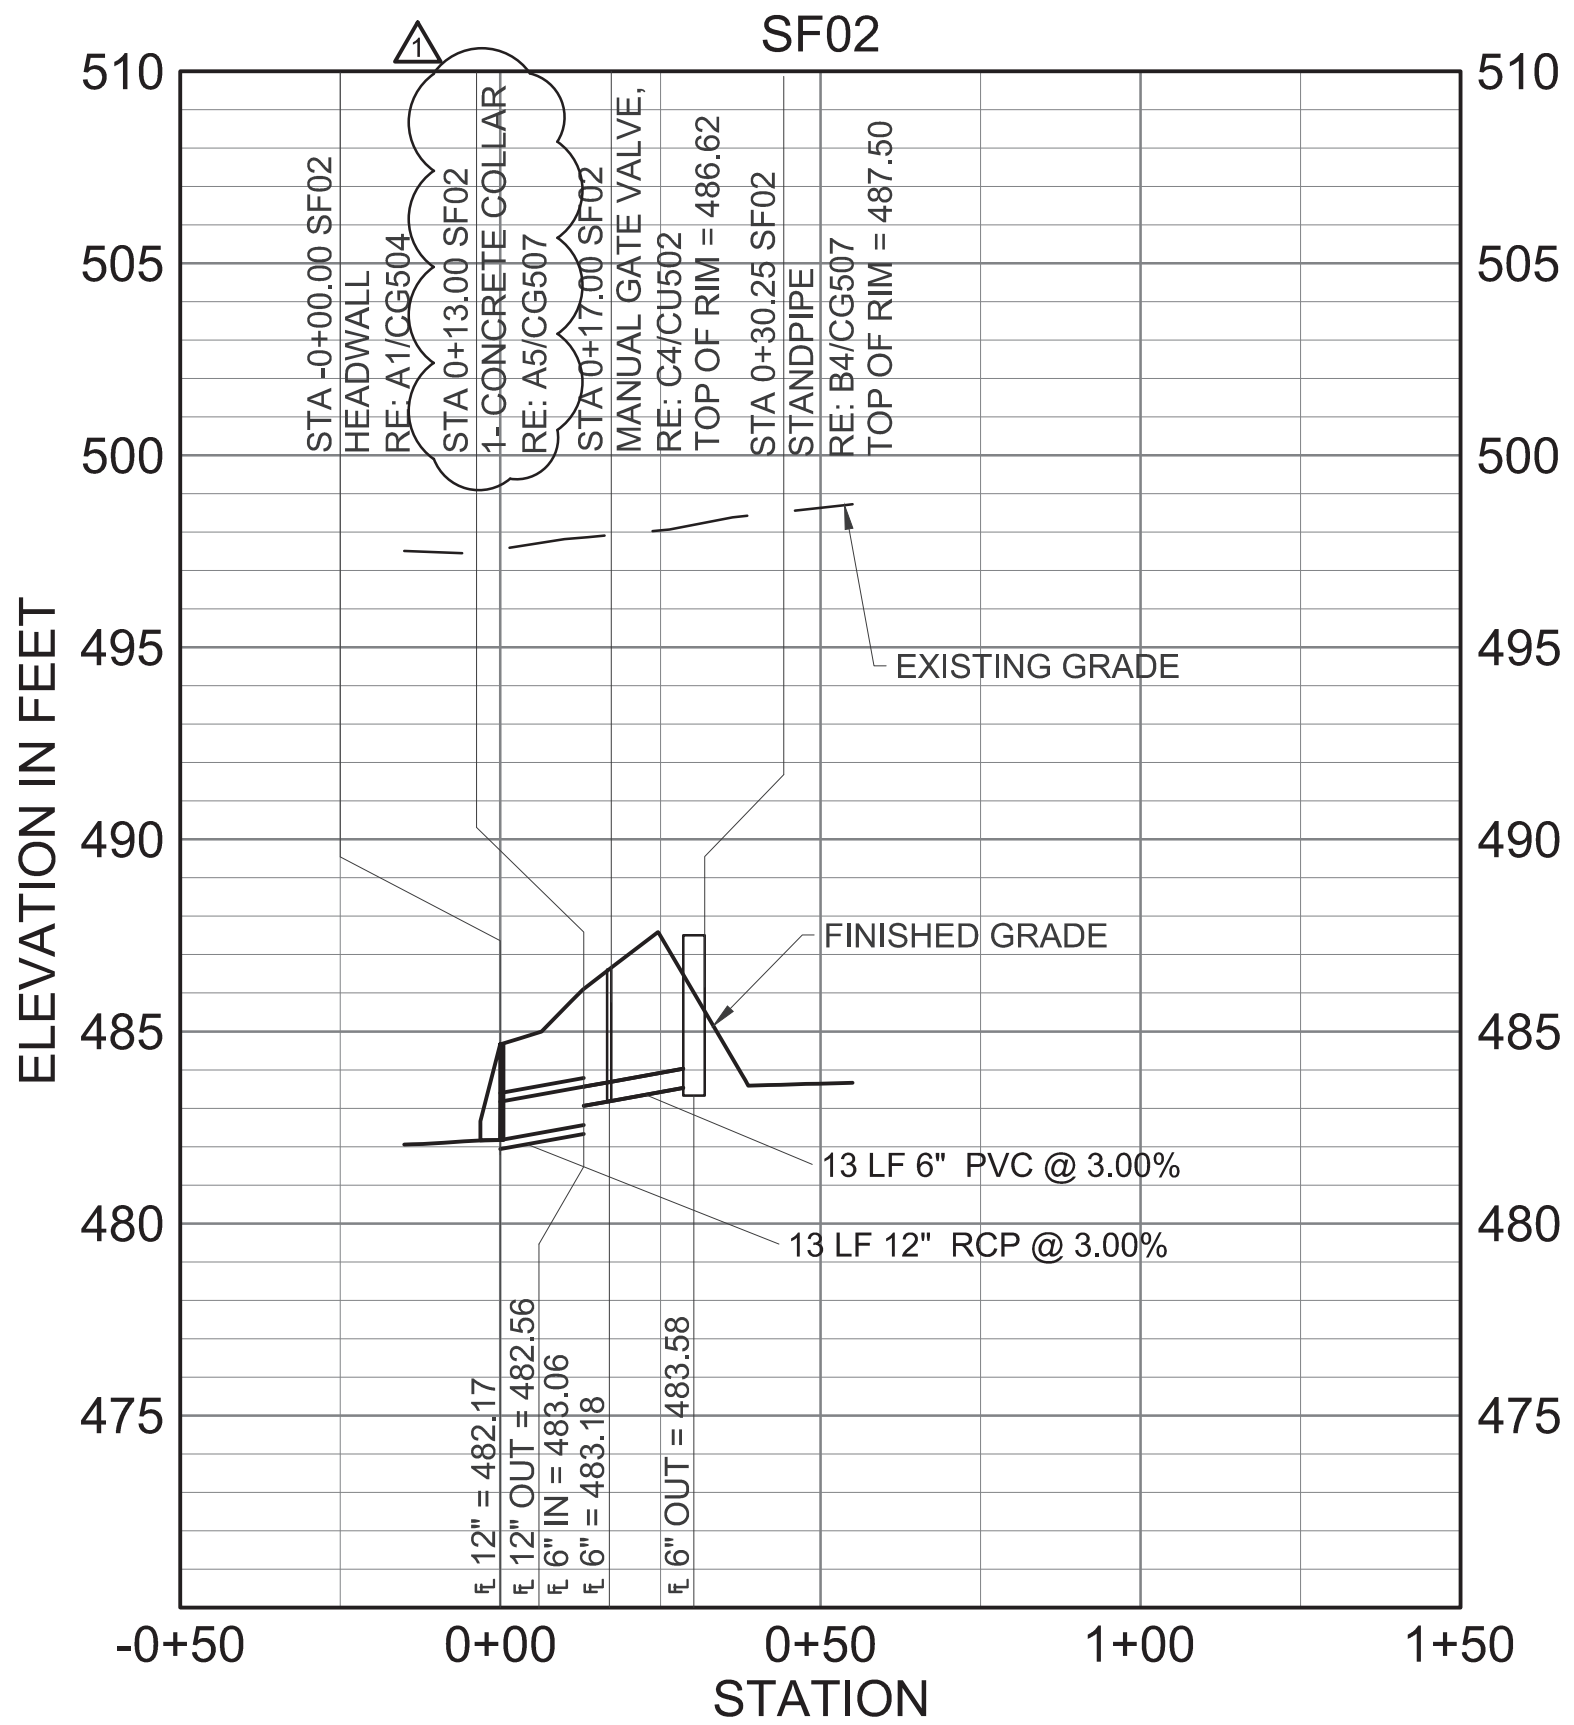

C3 DRAINAGE PROFILES - SF02
SCALE: HORIZONTAL 1" = 30'
VERTICAL 1" = 5'

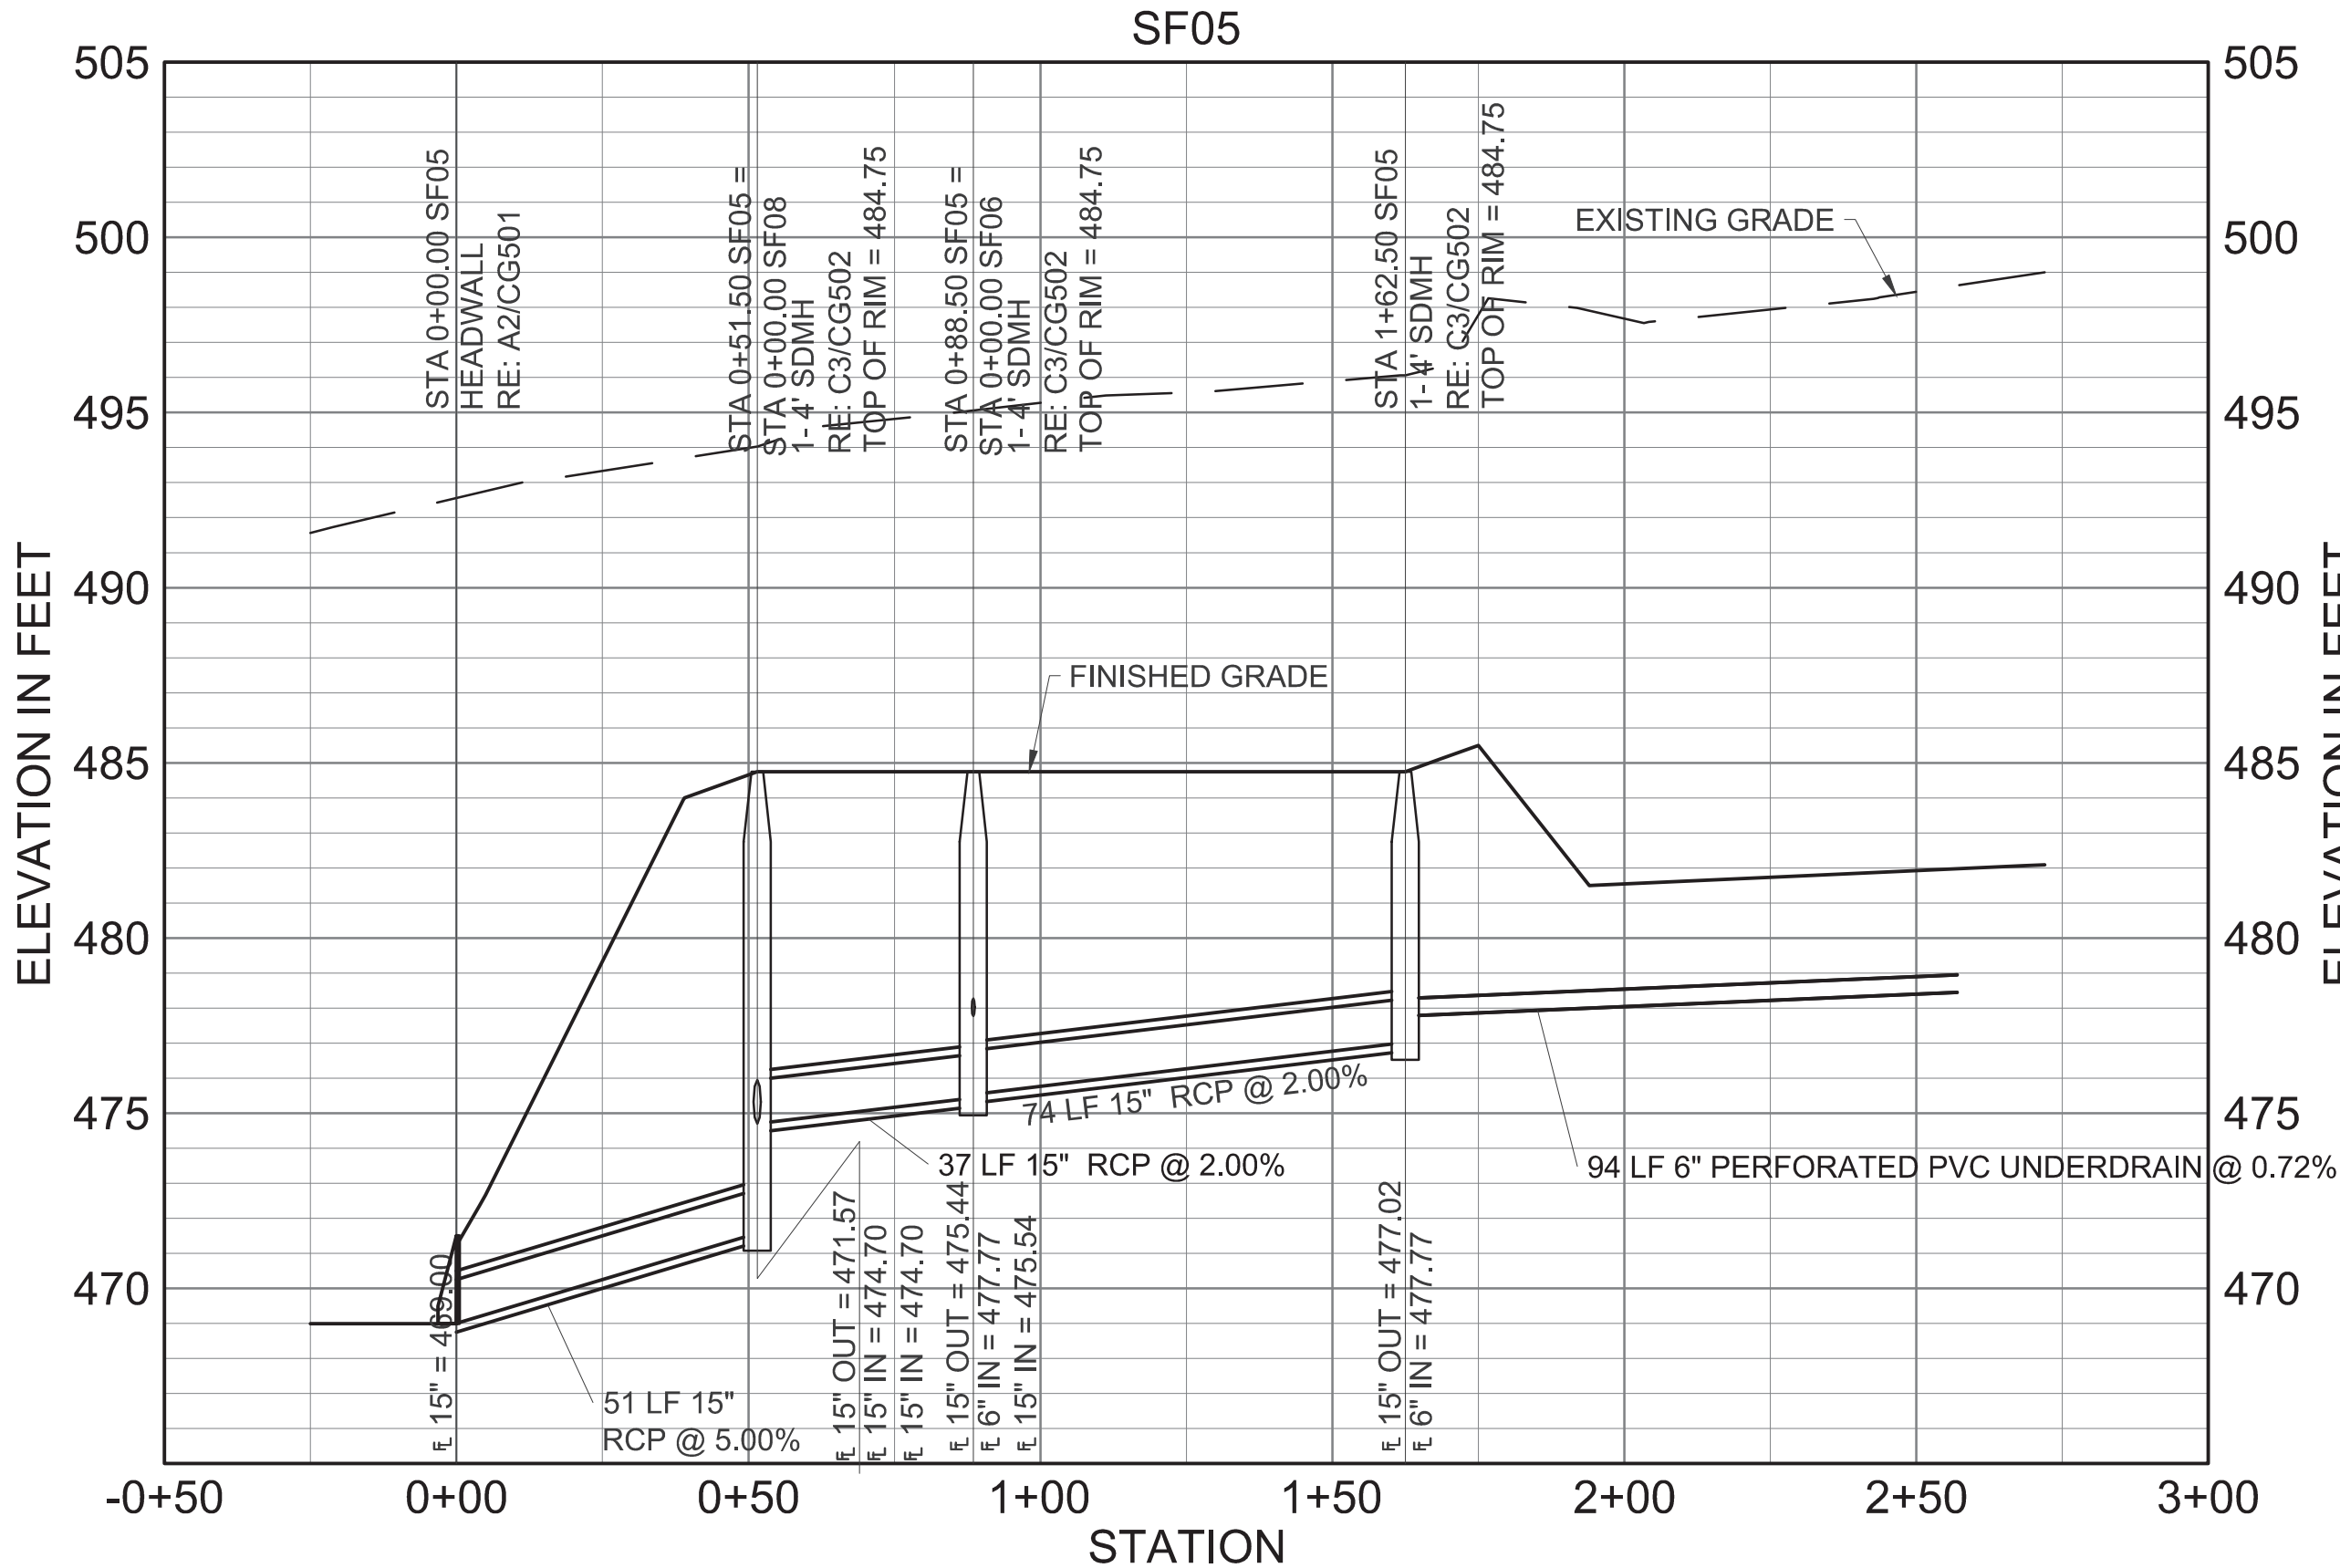

A3 DRAINAGE PROFILES - SF05
SCALE: HORIZONTAL 1" = 30'
VERTICAL 1" = 5'

3


3

D


C

B

A

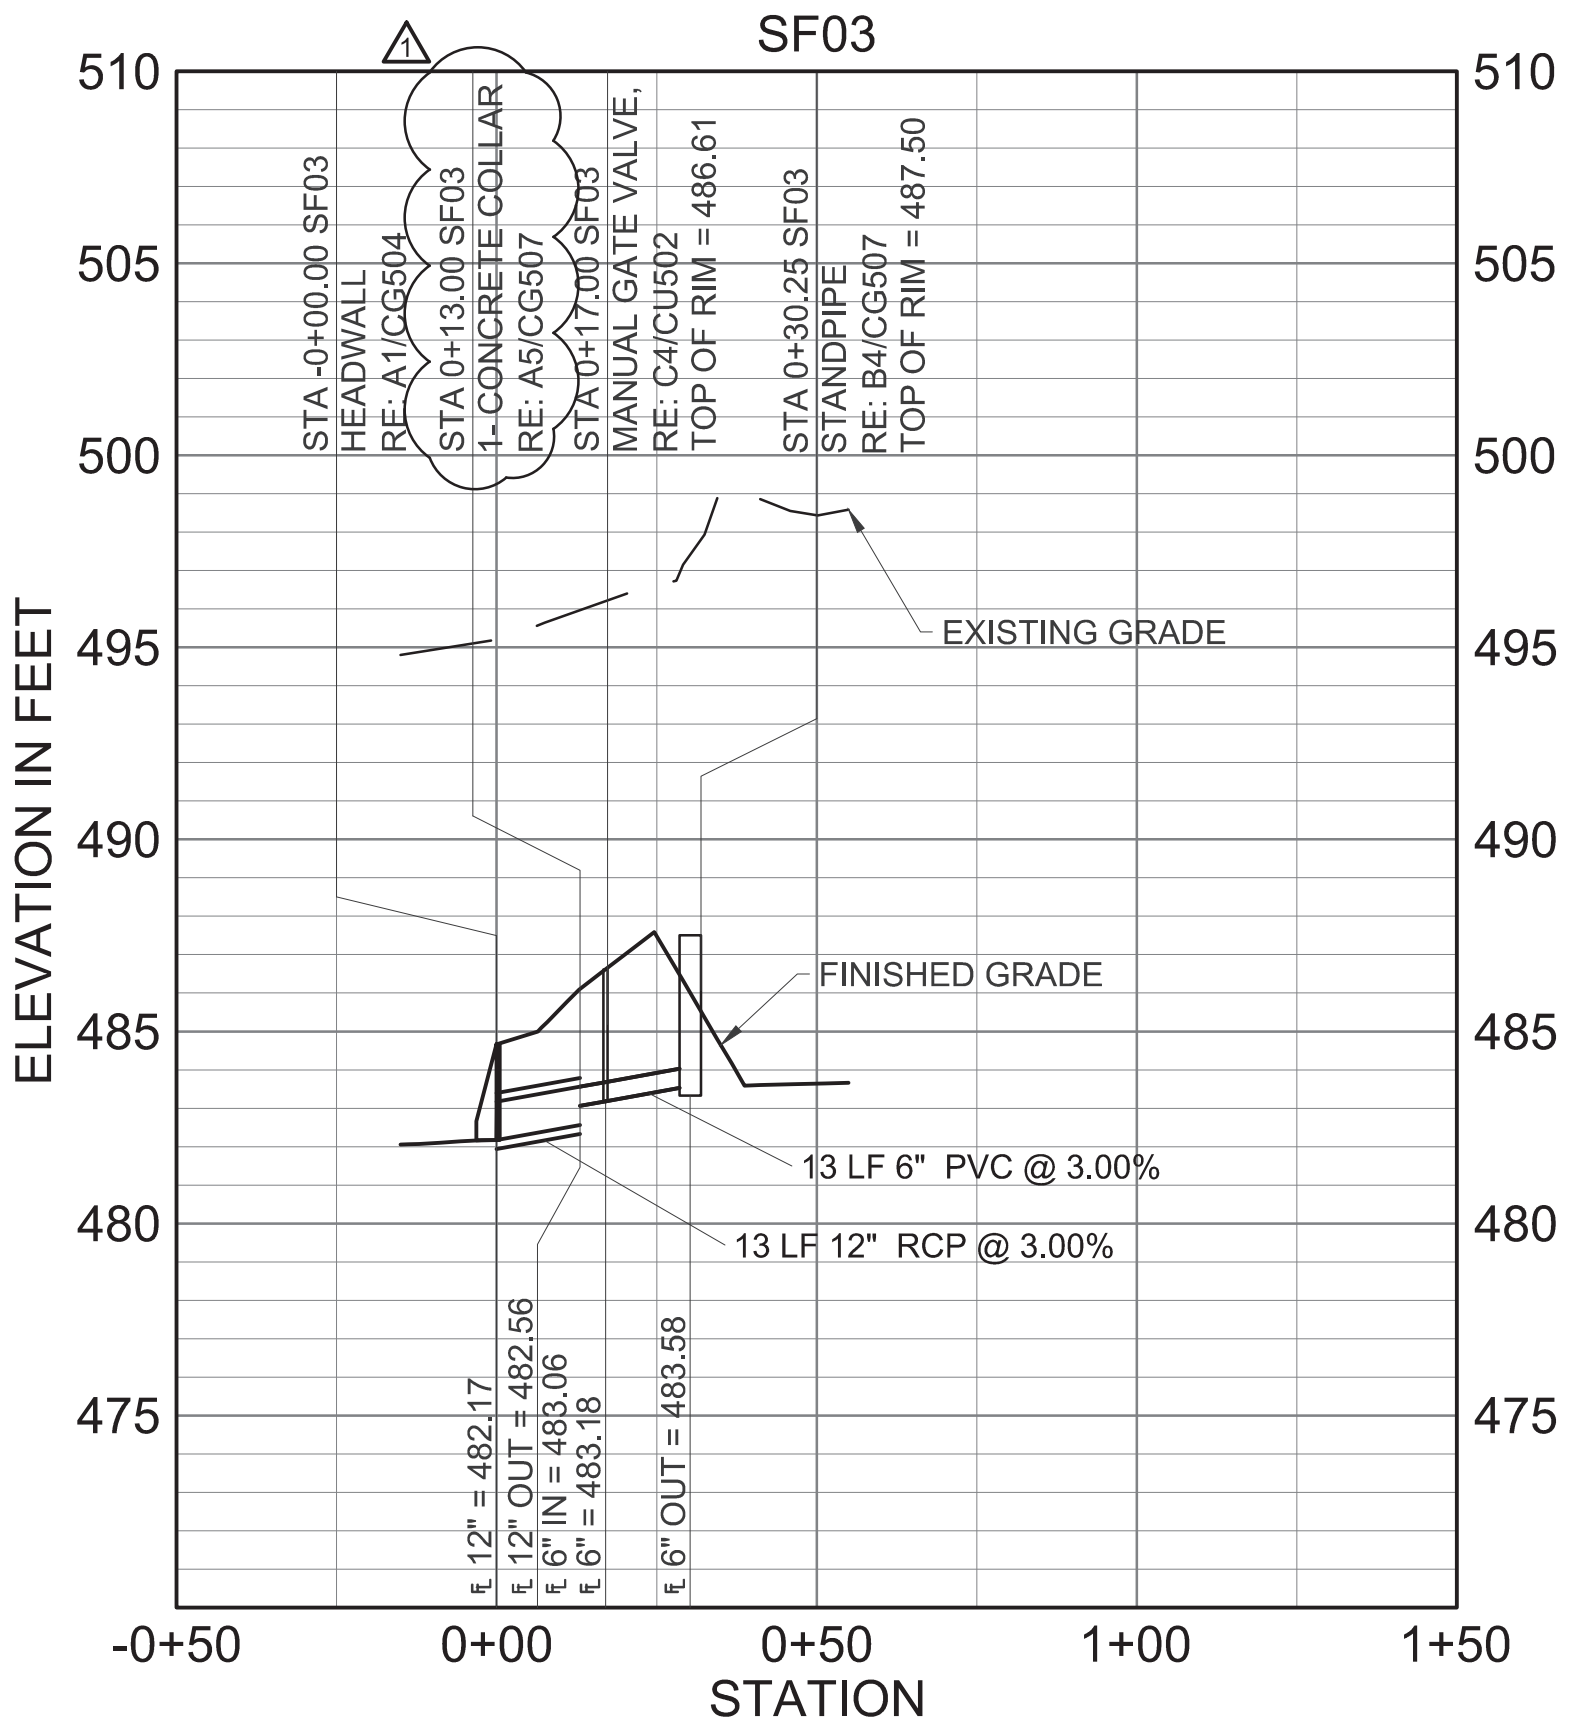

C4 DRAINAGE PROFILES - SF03
SCALE: HORIZONTAL 1" = 30'
VERTICAL 1" = 5'

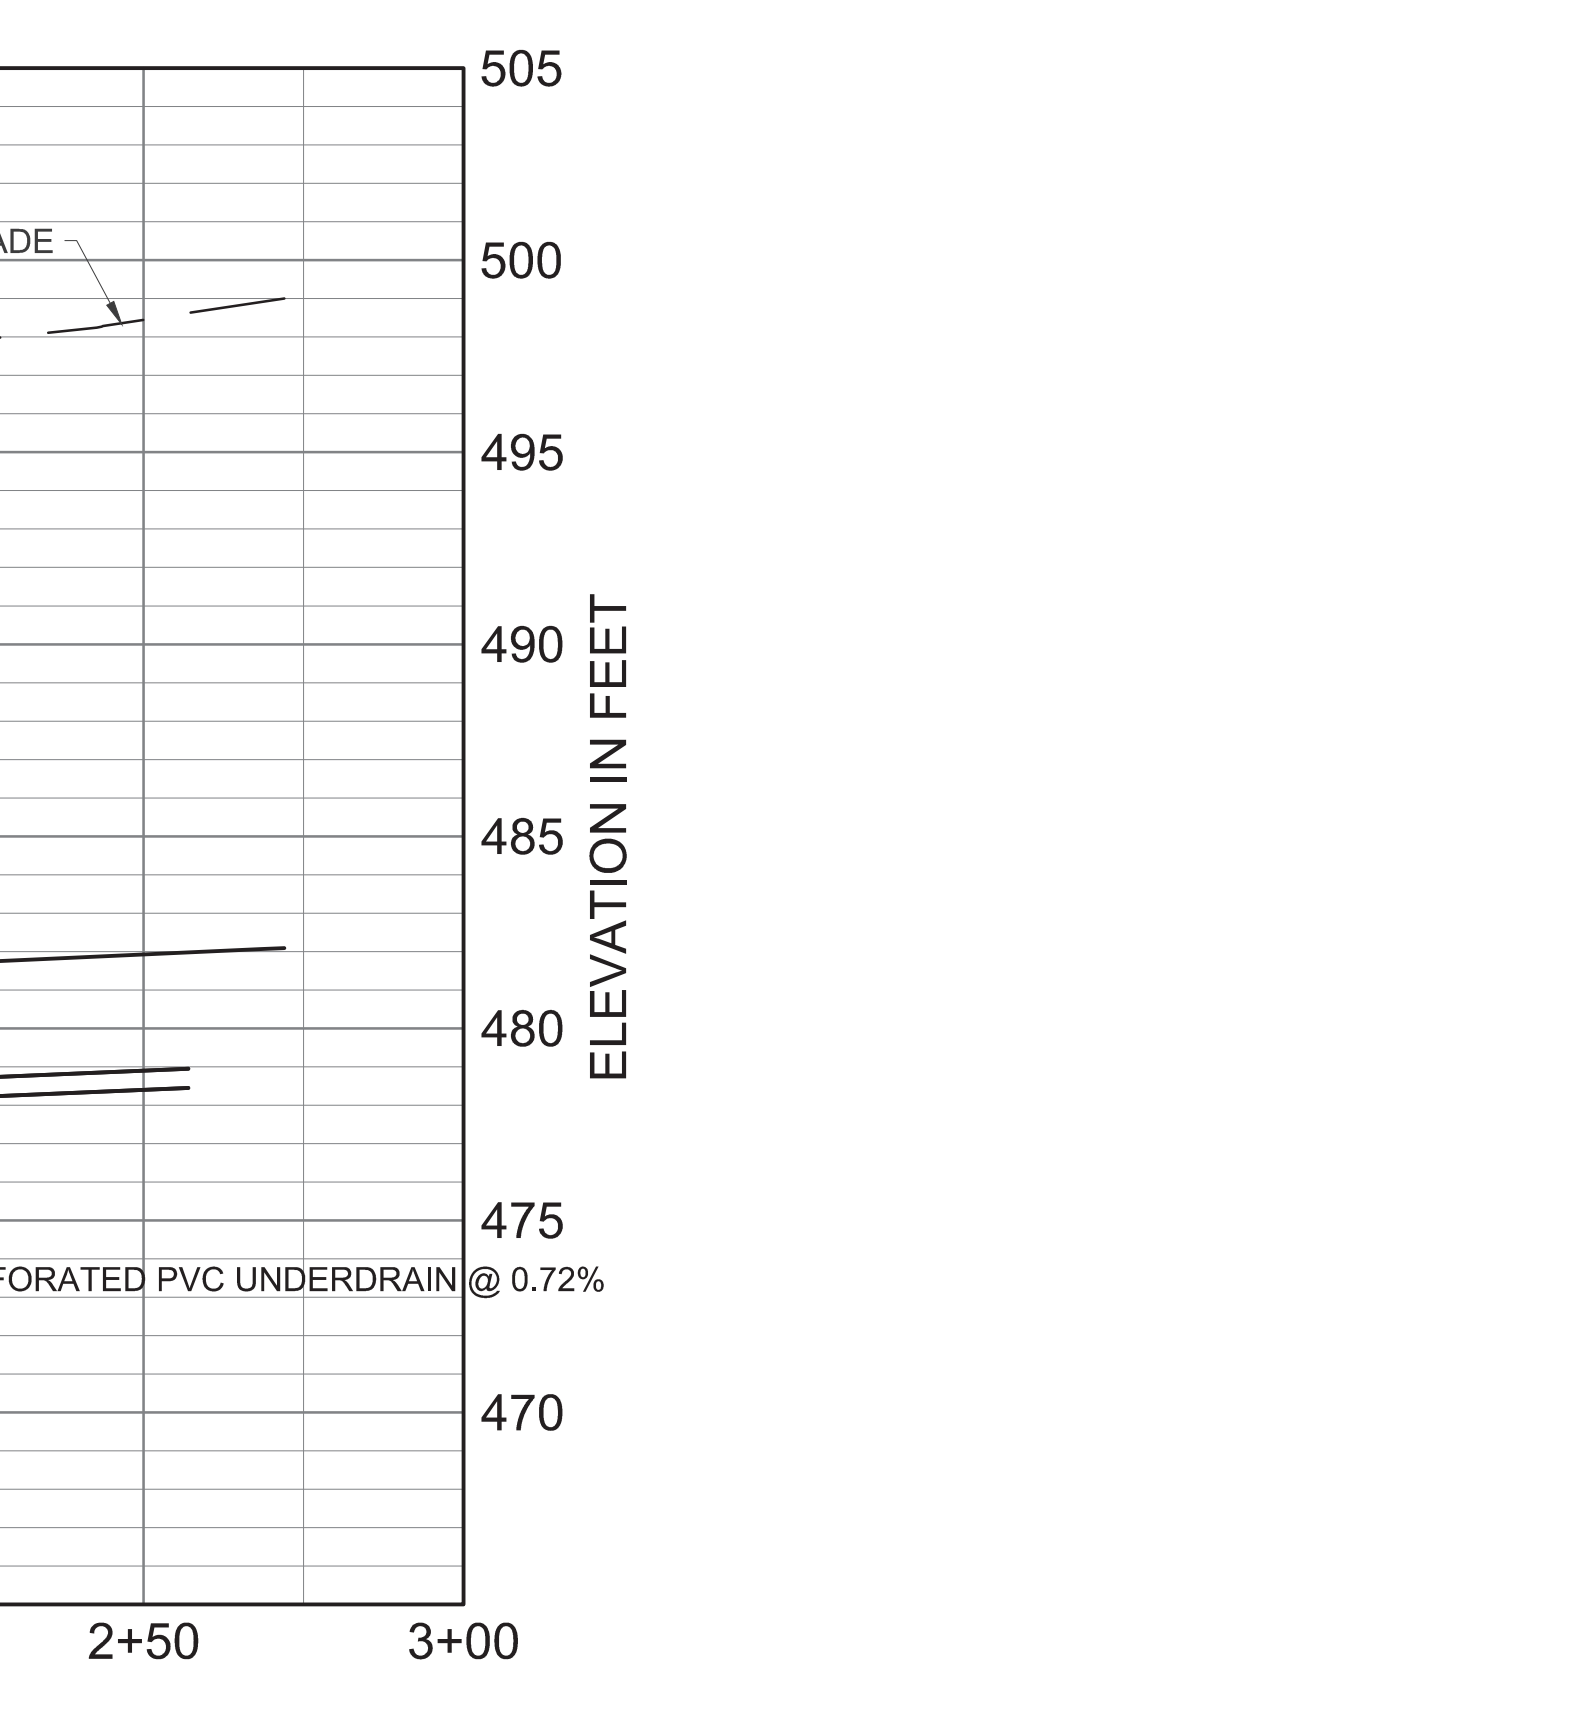

C4 DRAINAGE PROFILES - SF06
SCALE: HORIZONTAL 1" = 30'
VERTICAL 1" = 5'


5

5

0 2.5' 5' 10'
VERTICAL SCALE: 1"=5'

0 15' 30' 60'
HORIZONTAL SCALE: 1"=30'

SYMBOL	DESCRIPTION	DATE
1	AMEND. 0002 - REVISED DETAIL REFERENCE	03-MAR-26

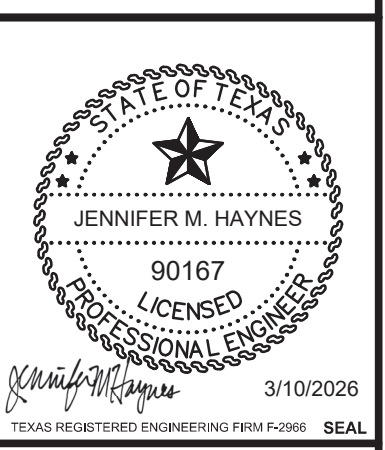

Jacobs **BURNS & MCDONNELL**
JACOBS: A JOINT VENTURE
1100 NORTH GLEBE ROAD
SUITE 500
ARLINGTON, VA 22201

APPROVED
DATE: 04/10/2026
FOR COMMANDER NAVFAC

ACTIVITY
AFMISC APPROVAL PER NAVFAC
SAT-TO CHECKLIST

SATISFACTORY TO DATE	31 DEC 2026	
DES: JMH	DRW: SMC	REV: ATM
PMIDM	KKK	
BRANCH MANAGER	SMK	
CHIEF ENGINEER/ARCH	SMK	
FIRE PROTECTION	RO	

DEPARTMENT OF THE NAVY
NAVFAC PACIFIC
ANDERSEN AIR FORCE BASE

NAVAL FACILITIES ENGINEERING SYSTEMS COMMAND
NAVAL FACILITIES ENGINEERING SYSTEMS COMMAND - PACIFIC
JOINT REGION WARRIORS (JRW)

GUAM

FY24 AJJY183012 (P-012),
PDI: NORTH AIRCRAFT PARKING RAMP


DRAINAGE PROFILES

SCALE: AS SHOWN
EPROJETS NO.: 1665555
CONSTR CONTROL NO.
NAVFAC DRAWING NO. 17361846
SHEET 223 OF 377

CG203

REDESIGN FINAL SUBMITTAL

FILE NAME: U:\BLDG\NAVFAC Pacific\03430603 - P-012 North Aircraft Parking Ramp\700 Working Documents\740.01 Civil\012_1665555_CU106.dwg
LAYOUT NAME: UTILITY PLAN - AREA 23
PLOTED: 03/16/2026 7:22pm
USER: CameroS

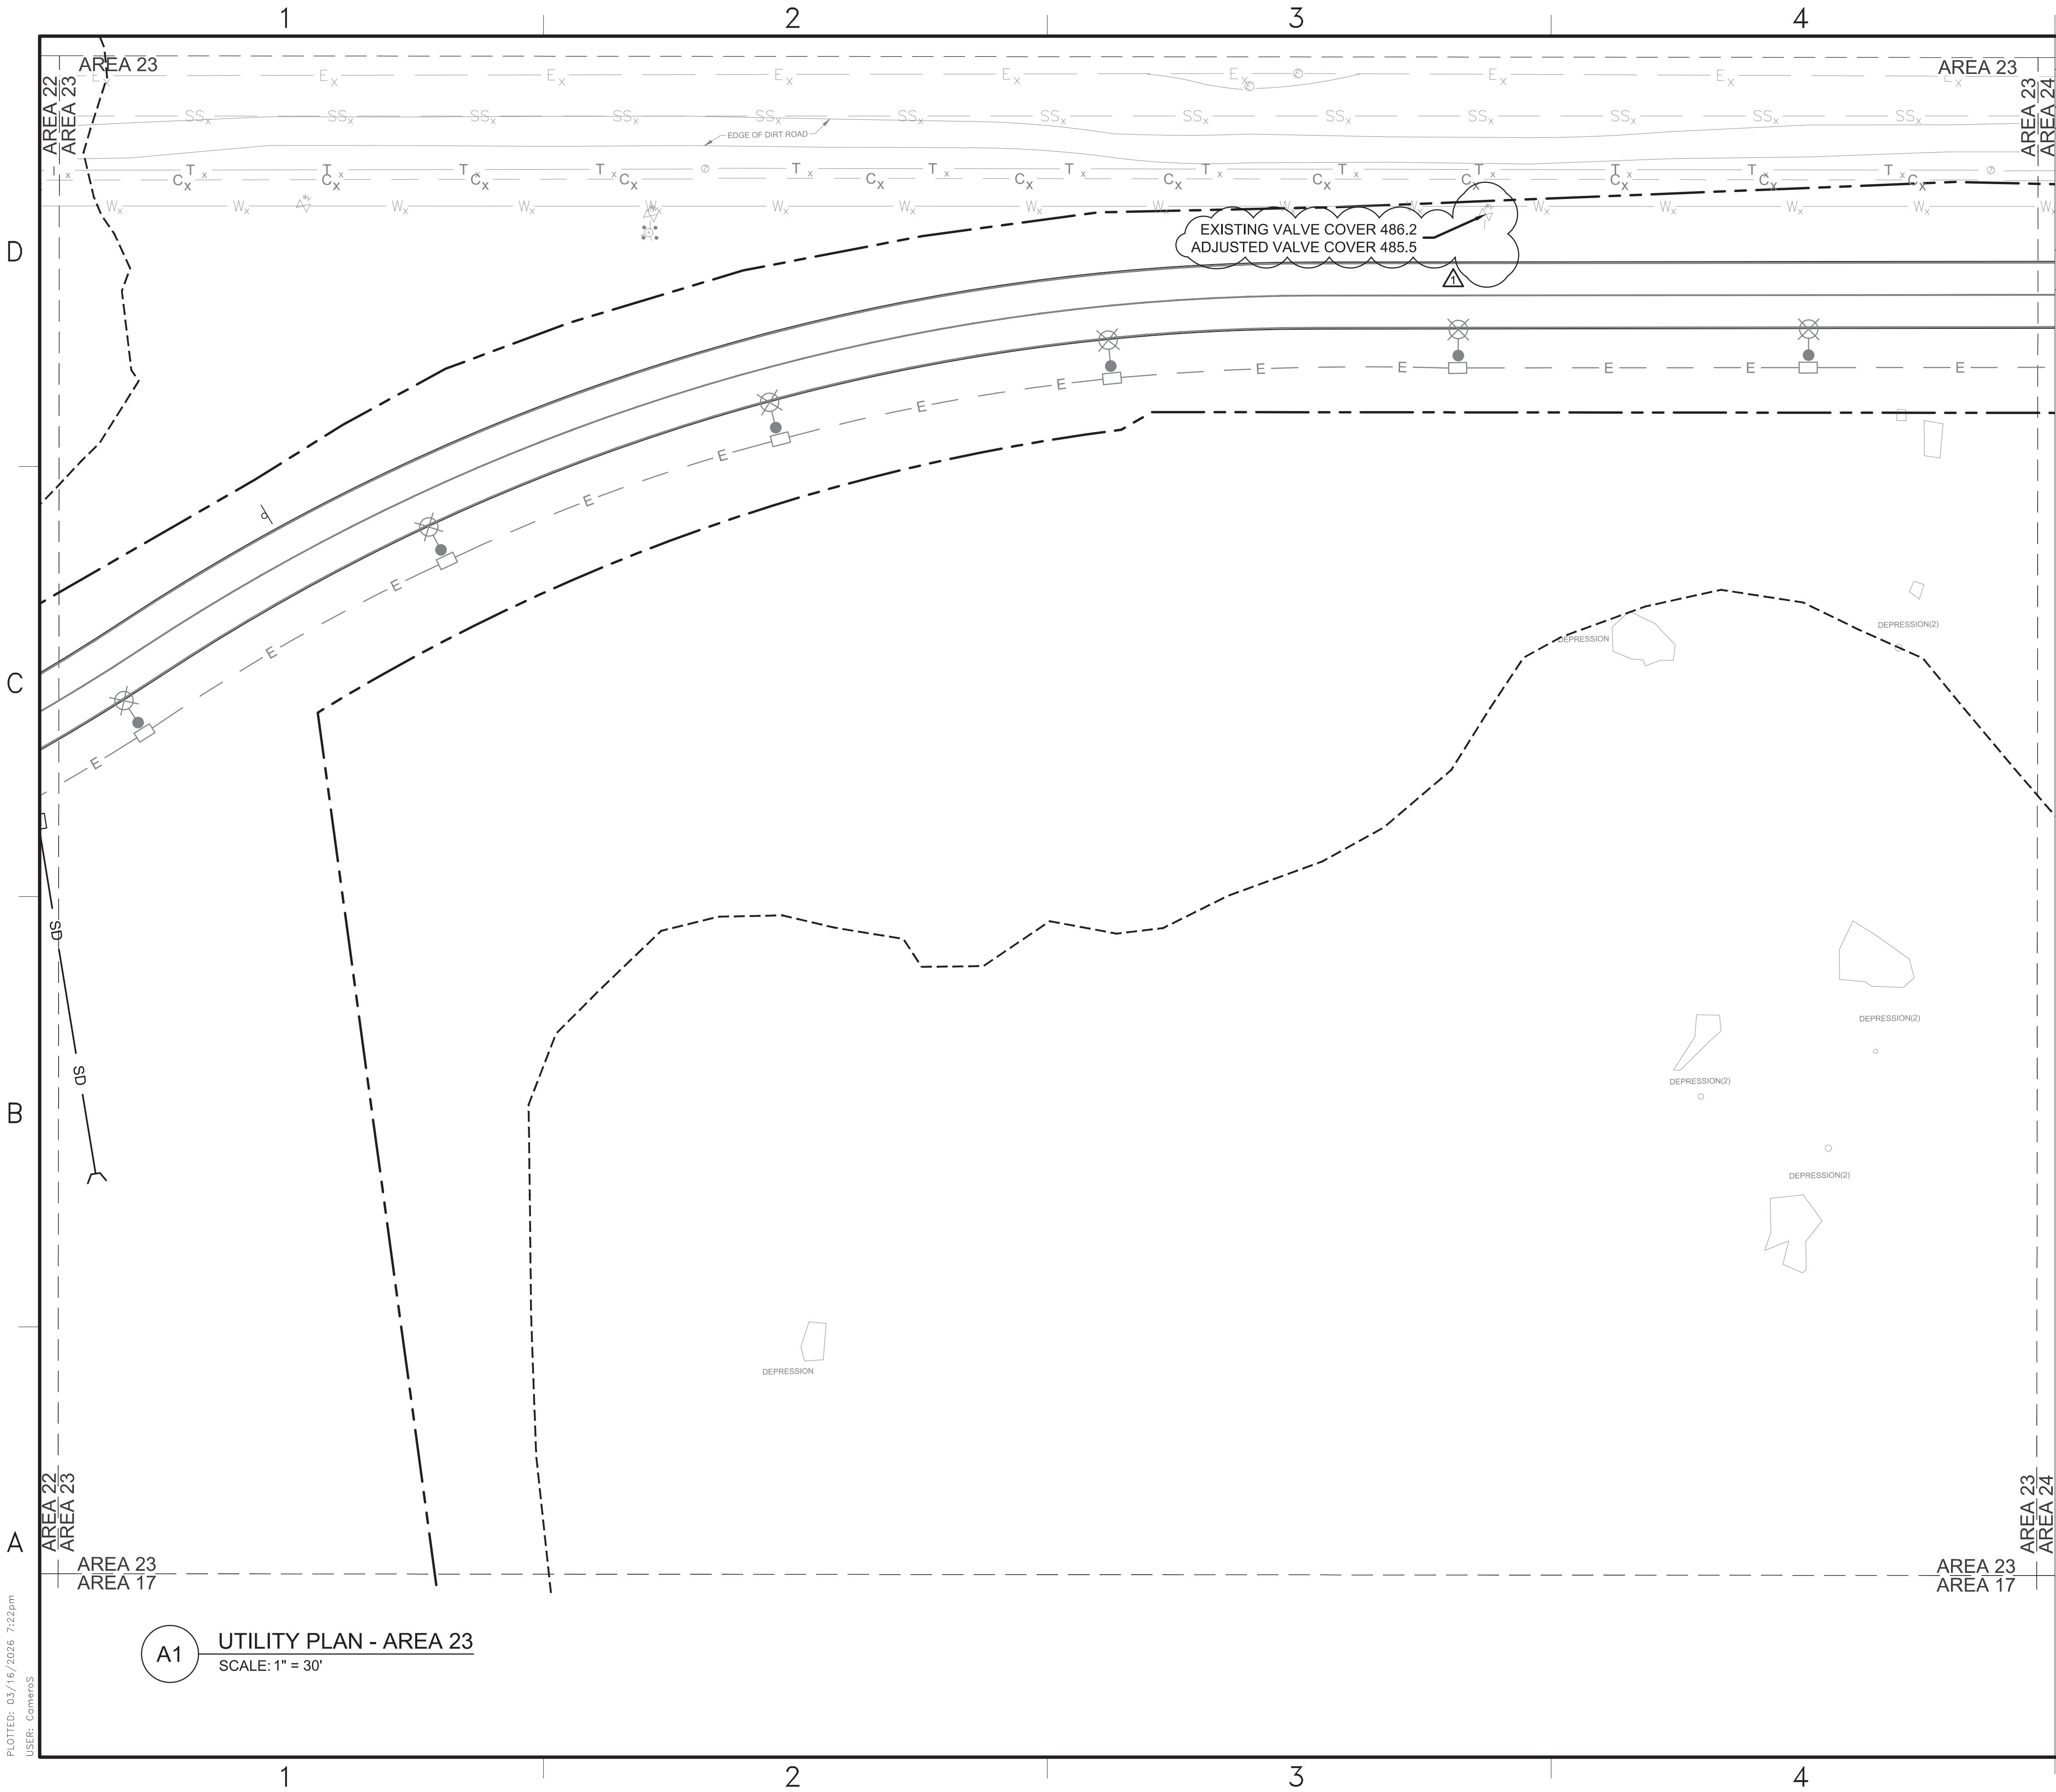


A1 UTILITY PLAN - AREA 23
SCALE: 1" = 30'

GENERAL NOTES

- A REFER TO SHEET ES101 - ES104 FOR SITE LIGHTING INFORMATION.
- B HORIZONTAL BENDS AND TEES REQUIRE THRUST BLOCKS


LEGEND

- LIMITS OF DISTURBANCE
- EXISTING SINKHOLE
- E --- UNDERGROUND ELECTRIC
- T_x --- EXISTING PHONE LINE
- W_x --- EXISTING WATERLINE
- SS_x --- EXISTING SANITARY SEWER
- E_x --- EXISTING UNDERGROUND ELECTRIC
- C_x --- EXISTING UNDERGROUND COMM.
- EXISTING FIRE HYDRANT
- EXISTING COMMUNICATION MANHOLE
- EXISTING ELECTRICAL MANHOLE
- EXISTING WATER VALVE

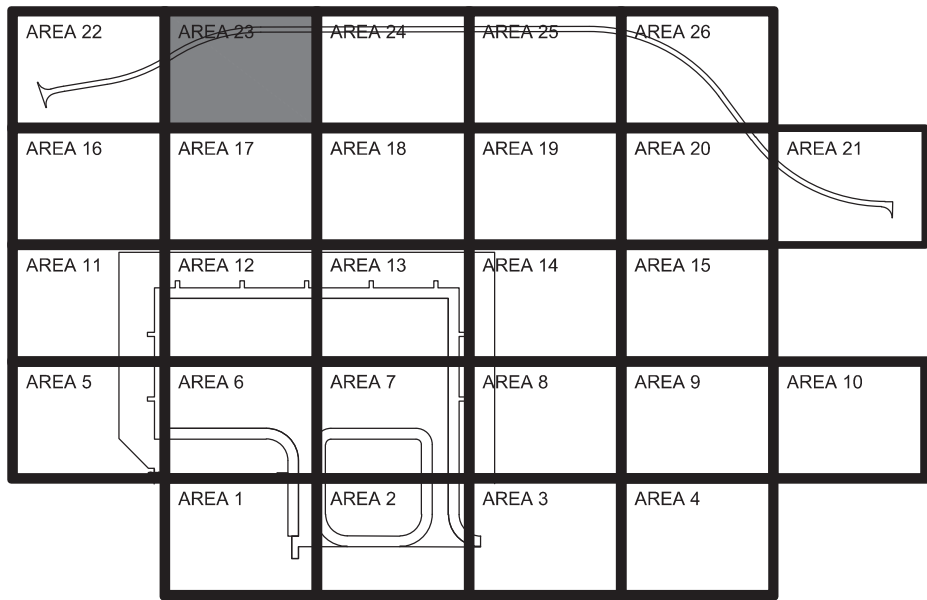


AREA 23 KEY PLAN

GRAPHIC SCALE

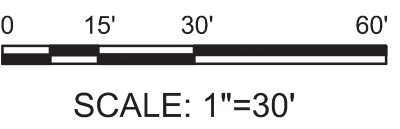

NORTH ARROW

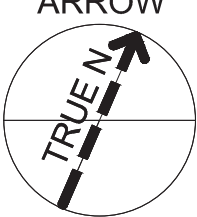

1	AMEND.002 - REVISED FHS	10-MAR-26	DATE
1	SYM DESCRIPTION		

JACOBS **BURNS**
MCDONNELL

JACOBSRAM, A JOINT VENTURE
1100 NORTH GLEBE ROAD
SUITE 500
ARLINGTON, VA 22201

A/E Contract No. N62162-24-2-0003
A/E Task Order No. N62162-24-2-0015
A/E No. 00000000

A/E INFO

APPROVED

Drawn By: *Camero S.*

FOR COMMANDER NAVFAC DATE 04/10/2026

ACTIVITY

AFMISC APPROVAL PER NAVFAC
SAT-TO CHECKLIST

SATISFACTORY TO DATE 31 DEC 2025

DES: JMH DRW: SMC REV: ATM

PM/DI KKK

BRANCH MANAGER SMK

CHIEF ENGINEER SMK

FIRE PROTECTION RO

DEPARTMENT OF THE NAVY
NAVAL FACILITIES ENGINEERING SYSTEMS COMMAND
NAVAL FACILITIES ENGINEERING SYSTEMS COMMAND - PACIFIC
JOINT REGION MARIANAS (JRM)

GUAM

FY24 AUJY183012 (P-012),
PDI: NORTH AIRCRAFT PARKING RAMP

UTILITY PLAN - AREA 23

SCALE: AS SHOWN

EPROJECTS NO.: 1665555

CONSTR CONTROL NO.


NAVFAC DRAWING NO.
17361868

SHEET 245 OF 377

CU106

REDESIGN FINAL SUBMITTAL

FILE NAME: U:\BLDG NAVFAC Pacific\03430603 - P-012 North Aircraft Parking Ramp\700 Working Documents\740 Sheets\740.01 Civil\012_1665555_CU107.dwg
LAYOUT NAME: UTILITY PLAN - AREA 24
PLOTTED: 03/16/2026 7:26pm
USER: CameroS


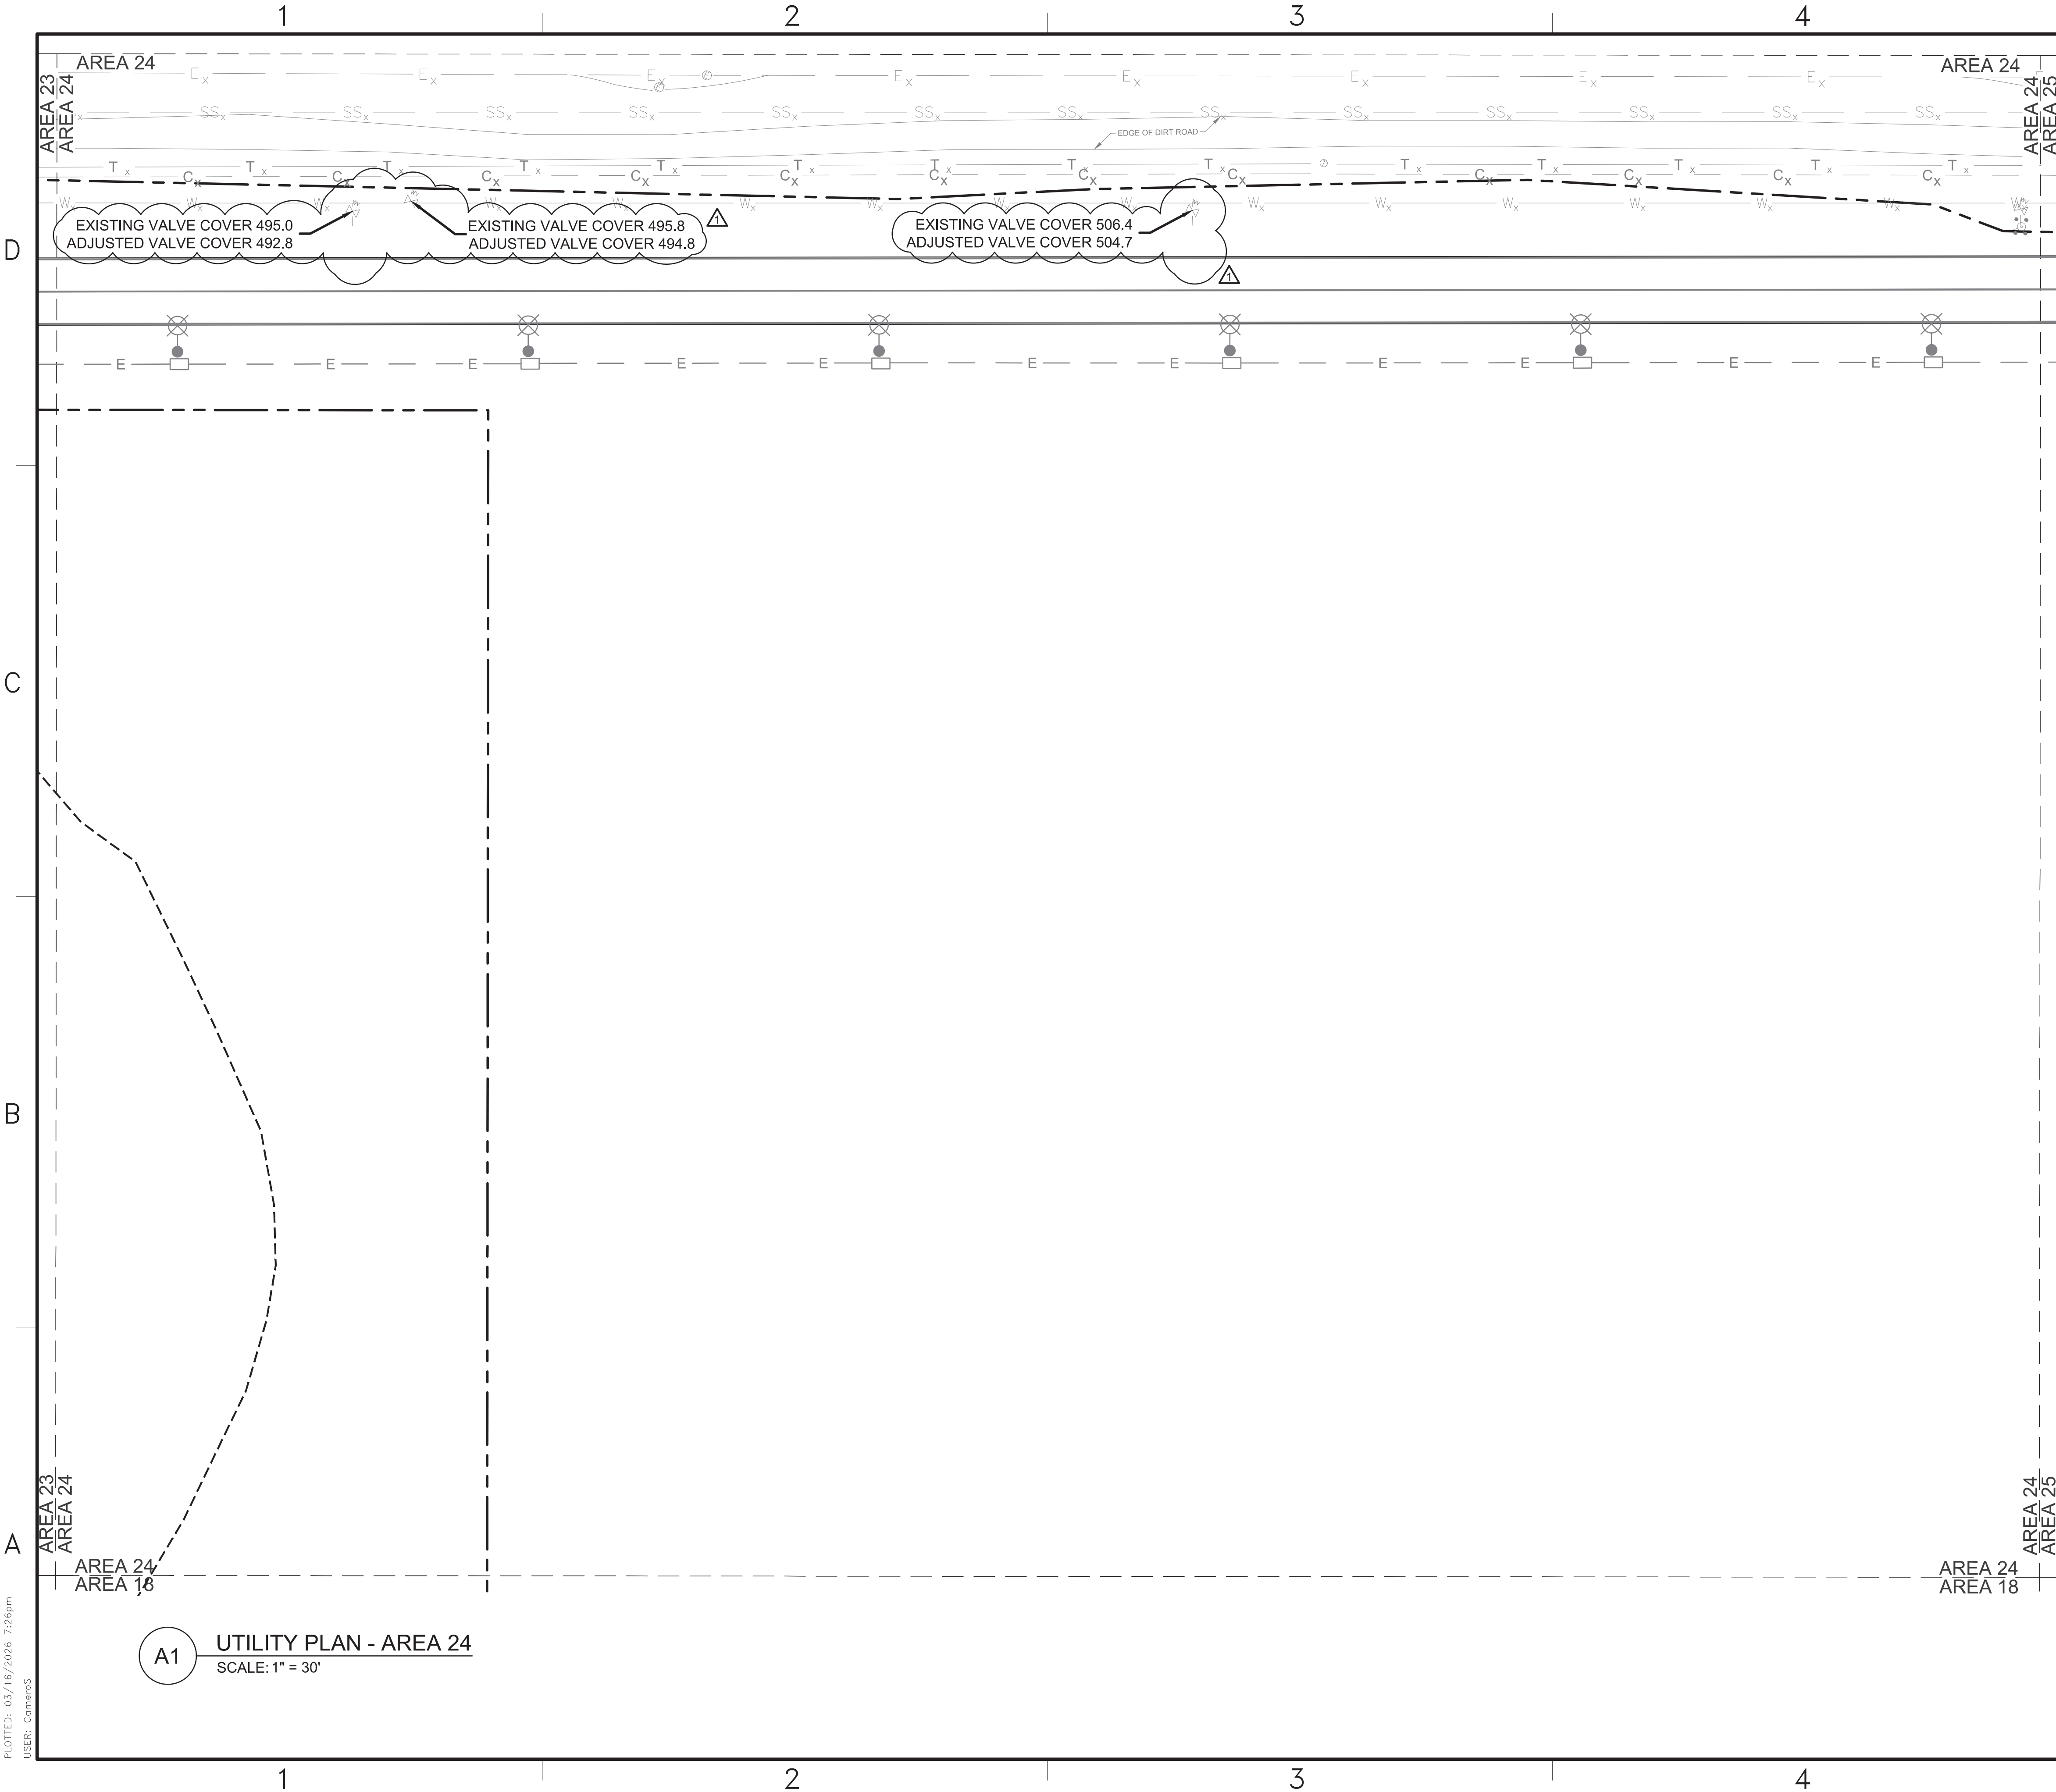


GENERAL NOTES

A REFER TO SHEET ES101 - ES104 FOR SITE LIGHTING INFORMATION.

B HORIZONTAL BENDS AND TEES REQUIRE THRUST BLOCKS

- LEGEND**
- LIMITS OF DISTURBANCE
 - - - EXISTING SINKHOLE
 - E - UNDERGROUND ELECTRIC
 - T_x - EXISTING PHONE LINE
 - W_x - EXISTING WATERLINE
 - SS_x - EXISTING SANITARY SEWER
 - E_x - EXISTING UNDERGROUND ELECTRIC
 - C_x - EXISTING UNDERGROUND COMM.
 - ☼ EXISTING FIRE HYDRANT
 - ⊙ EXISTING COMMUNICATION MANHOLE
 - ⊗ EXISTING ELECTRICAL MANHOLE
 - ⊠ EXISTING WATER VALVE

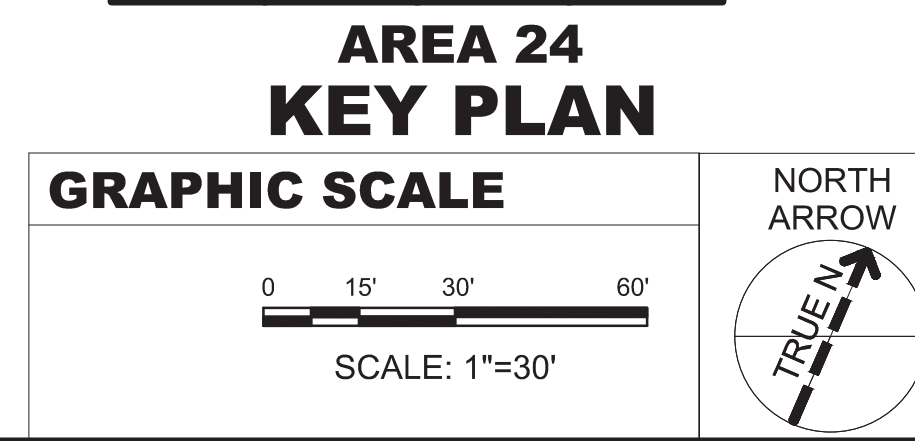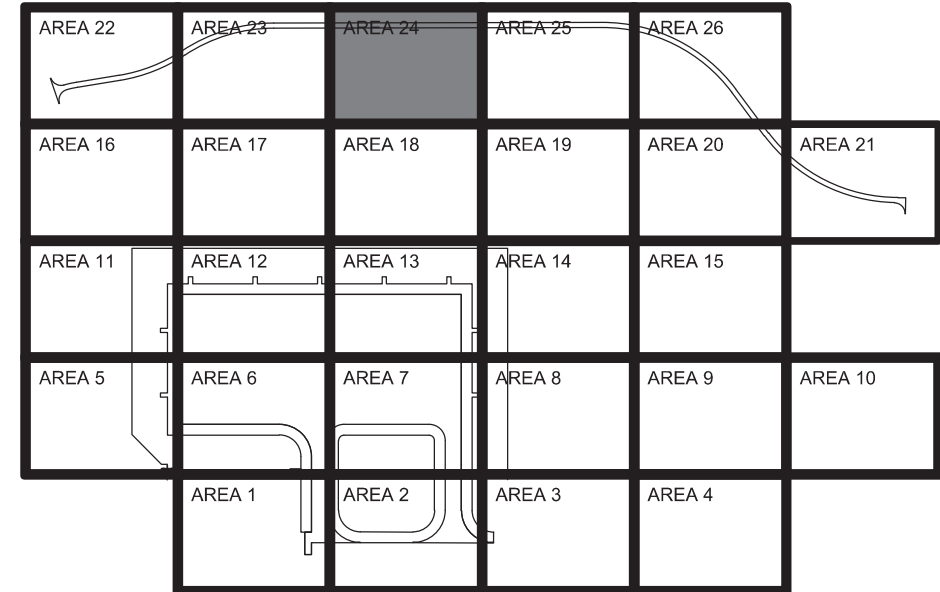

1	AMEND.002 - REVISED FHS	10-MAR-26	DATE
1	SYM DESCRIPTION		

JACOBS JACOBSRAM A JOINT VENTURE
1100 NORTH GLEBE ROAD
SUITE 500
ARLINGTON, VA 22201

A/E Contract No. N62162-25-D-0002
A/E Task Order No. N62162-25-D-0002
A/E No. 00000000

APPROVED

DATE: 04/10/2026

FOR COMMANDER NAVFAC

ACTIVITY

AFMISC APPROVAL PER NAVFAC SAT-TO CHECKLIST

SATISFACTORY TO DATE 31 DEC 2025

DES: JMH DRW: SMC REV: ATM

PM/DM KKK

BRANCH MANAGER SMK

CHIEF ENGINEER SMK

FIRE PROTECTION RO

DEPARTMENT OF THE NAVY
NAVAL FACILITIES ENGINEERING SYSTEMS COMMAND
NAVAL FACILITIES ENGINEERING SYSTEMS COMMAND - PACIFIC
JOINT REGION MARIANAS (JRM)
GUAM


FY24 AJJY183012 (P-012)
PDI: NORTH AIRCRAFT PARKING RAMP

UTILITY PLAN - AREA 24

CU107

IF SHEET IS LESS THAN 22" X 34"
REDUCED PRINT. USE GRAPHIC SCALES

FILE NAME: U:\BLOG\NAVFAC Pacific\03430603 - P-012 North Aircraft Parking Ramp\700 Working Documents\740.01 Civil\012_1665555_CU108.dwg
LAYOUT NAME: UTILITY PLAN - AREA 25
PLOTTED: 03/09/2026 2:28pm
USER: CameroS

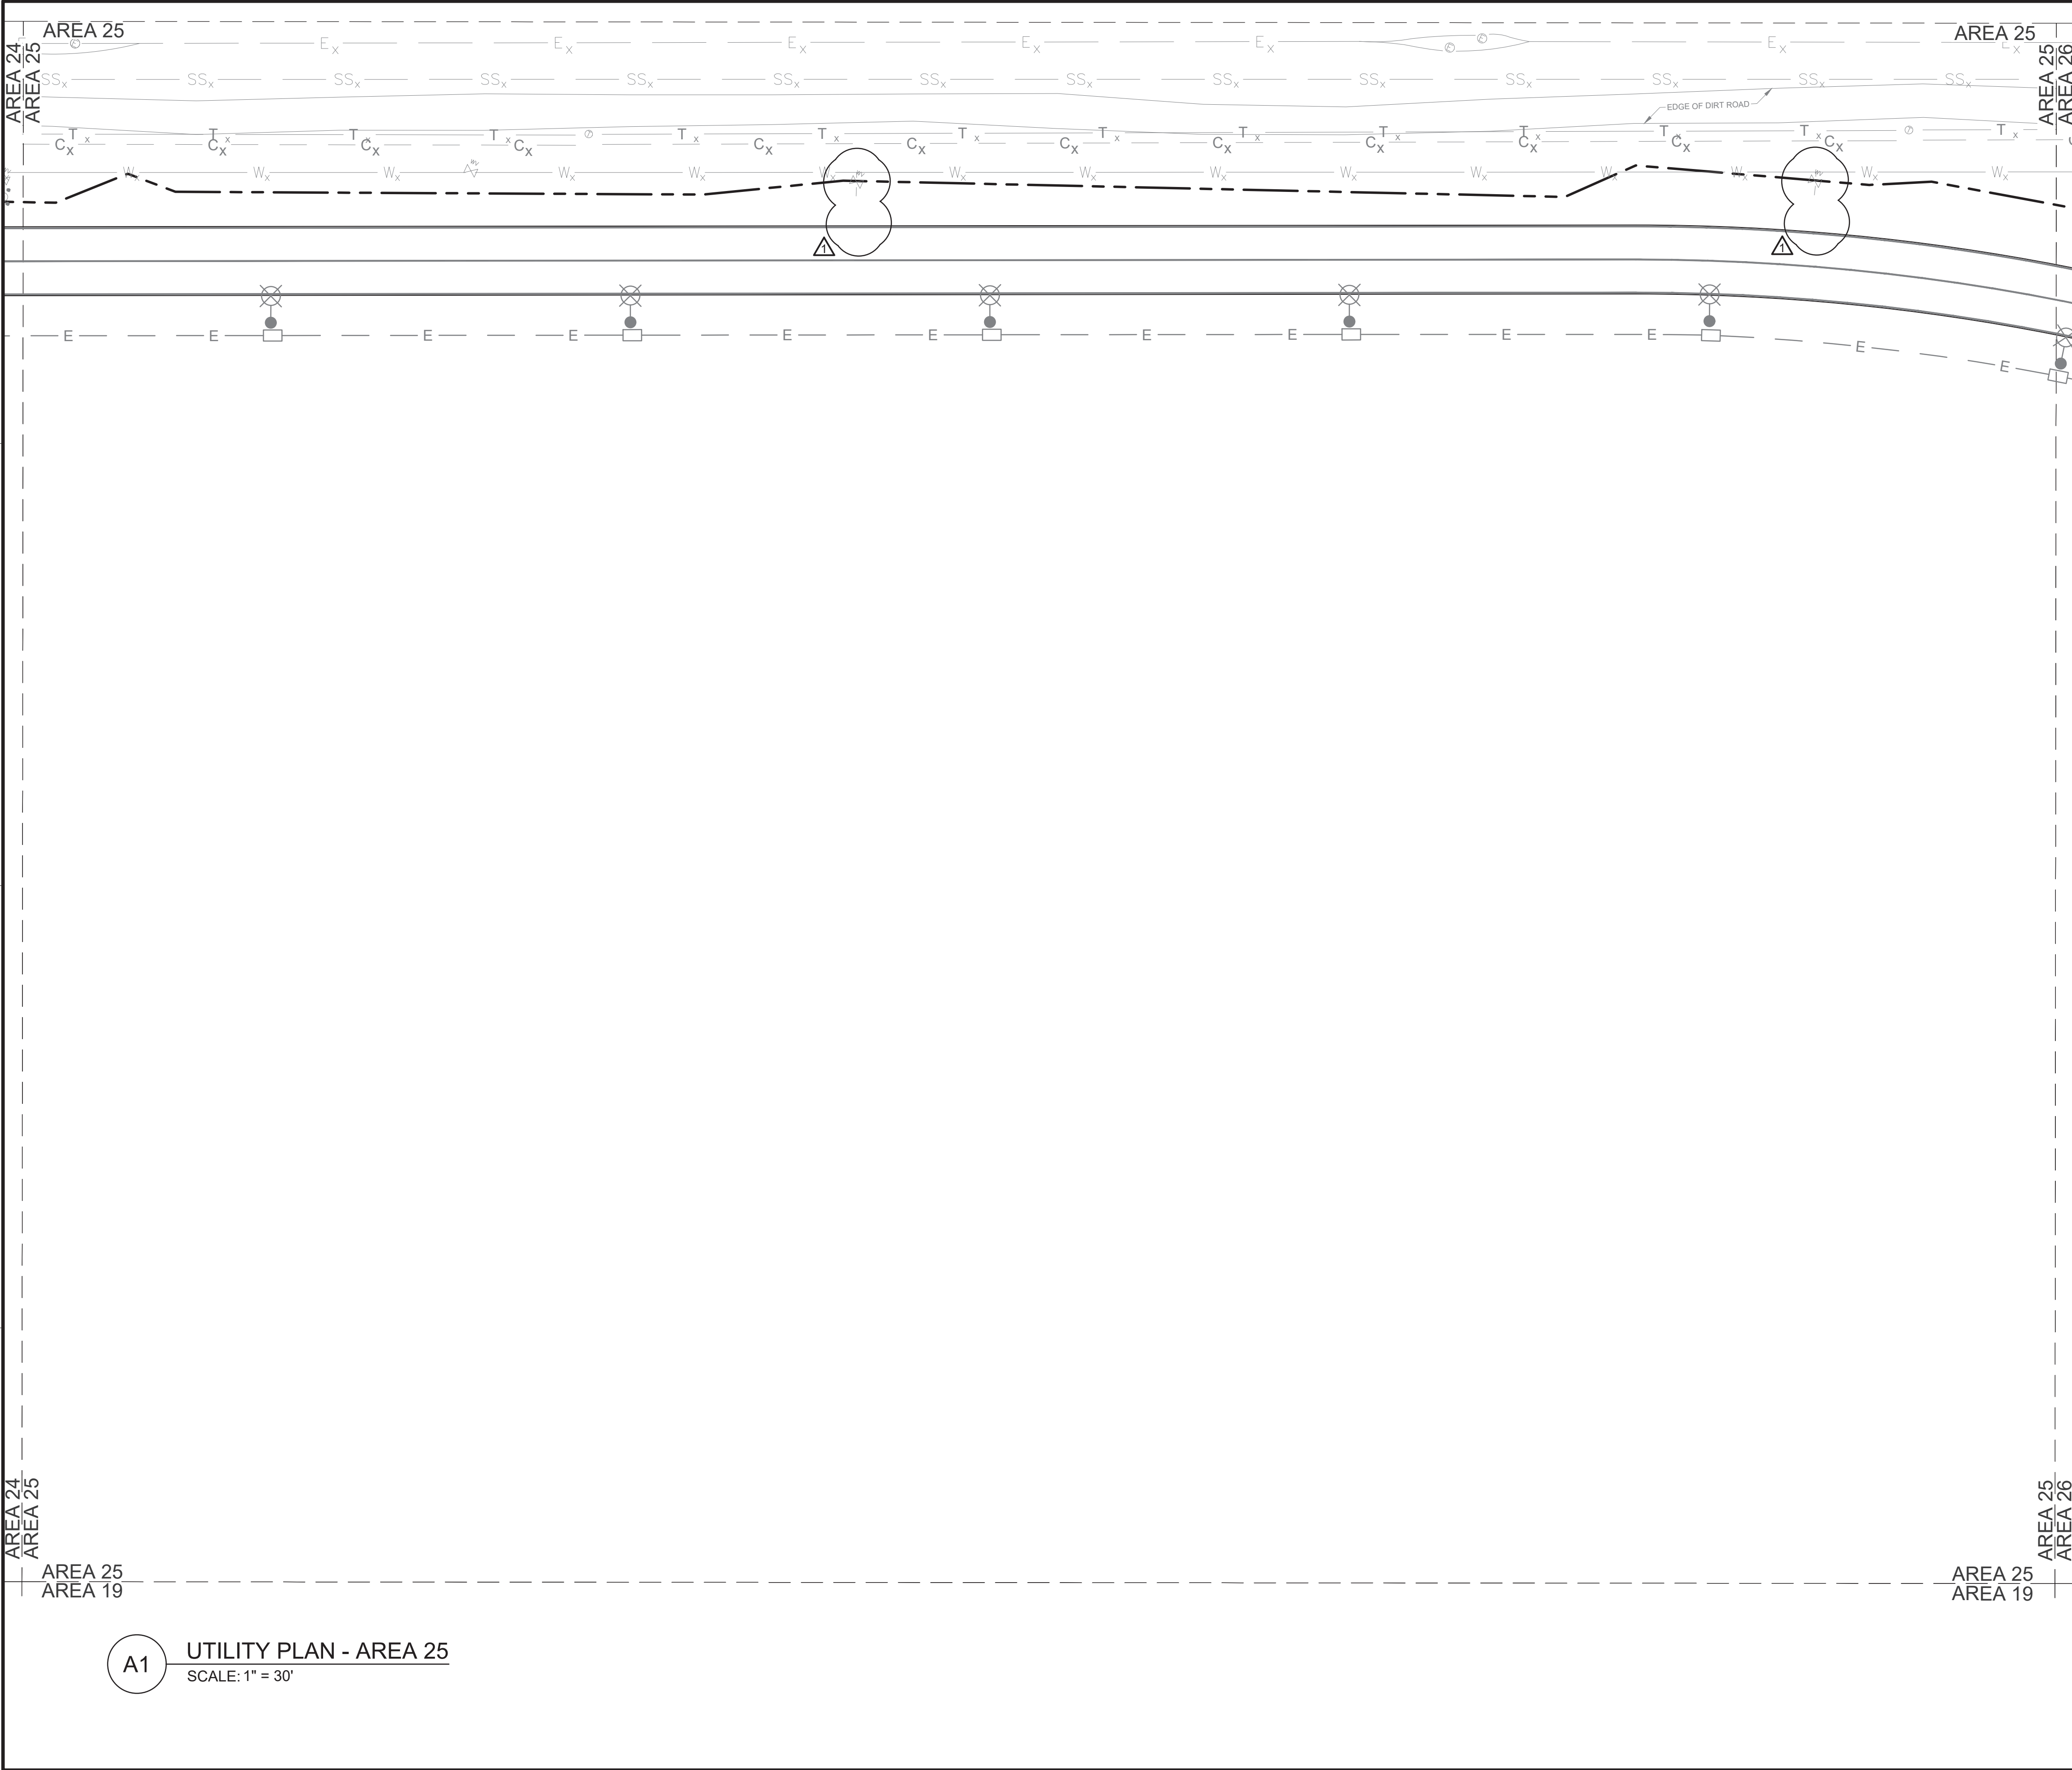

GENERAL NOTES

A REFER TO SHEET ES101 - ES104 FOR SITE LIGHTING INFORMATION.

B HORIZONTAL BENDS AND TEES REQUIRE THRUST BLOCKS

LEGEND

--- LIMITS OF DISTURBANCE

--- E --- UNDERGROUND ELECTRIC

--- T_x --- EXISTING PHONE LINE

--- W_x --- EXISTING WATERLINE

--- SS_x --- EXISTING SANITARY SEWER

--- E_x --- EXISTING UNDERGROUND ELECTRIC

--- C_x --- EXISTING UNDERGROUND COMM.

Existing Communication Manhole

Existing Electrical Manhole

Existing Water Valve

AREA 25
KEY PLAN

GRAPHIC SCALE

0 15' 30' 60'

SCALE: 1"=30'

NORTH ARROW

TRUE N

STATE OF TEXAS

JENNIFER M. HAYNES

90167

LICENSED PROFESSIONAL ENGINEER

3/10/2026

SEAL

JACOBS

BURNS & MCDONNELL

JACOBSRAM A JOINT VENTURE

1100 NORTH GLEBE ROAD

SUITE 500

ARLINGTON, VA 22201

A/E Contract No. 160742-25-0-0003

A/E Task Order No. 160742-25-0-0003

A/E No. 00000000

A/E INFO

APPROVED

DATE 04/10/2026

FOR COMMANDER NAVFAC

DATE 04/10/2026

ACTIVITY

AFMISC APPROVAL PER NAVFAC SAT-TO CHECKLIST

SATISFACTORY TO DATE

31 DEC 2026

DES: JMH

DRW: SMC

REV: ATM

PMIDM

KKK

BRANCH MANAGER

SMK

CHIEF ENGINEER

SMK

FIRE PROTECTION

RO

DEPARTMENT OF THE NAVY

NAVAL FACILITIES ENGINEERING SYSTEMS COMMAND

NAVAL FACILITIES ENGINEERING SYSTEMS COMMAND - PACIFIC

JOINT REGION MARIANAS (JRM)

GUAM

FY24 AJJY183012 (P-012)

PDI: NORTH AIRCRAFT PARKING RAMP

UTILITY PLAN - AREA 25

SCALE: AS SHOWN

EPROJECTS NO.: 1665555

CONSTR CONTROL NO.

NAVFAC DRAWING NO. 17361870

SHEET 247 OF 377

CU108


REDESIGN FINAL SUBMITTAL

FILE NAME: U:\BLOG\NAVFAC Pacific\03430603 -- P-012 North Aircraft Parking Ramp\700 Working Documents\740 Sheets\740.01 Civil\012_1665555_CU203.dwg

LAYOUT NAME: UTILITY PROFILES

PLOTTED: 03/09/2026 12:36pm

USER: CameroS

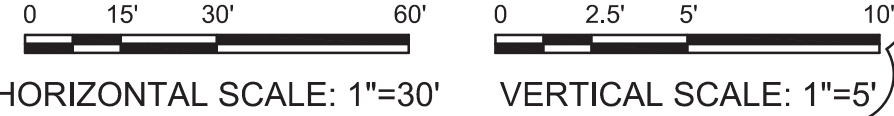

CU203

SHEET 251 OF 377

NAVFAC DRAWING NO. 17361874

CONSTR CONTROL NO.

EPROJECTS NO.: 1665555

SCALE: AS SHOWN

UTILITY PROFILES

PDI: NORTH AIRCRAFT PARKING RAMP

FY24 AJJY183012 (P-012),

ANDERSEN AIR FORCE BASE

NAVFAC PACIFIC

NAVAL FACILITIES ENGINEERING SYSTEMS COMMAND ~ PACIFIC

NAVAL FACILITIES ENGINEERING SYSTEMS COMMAND

DEPARTMENT OF THE NAVY

CHIEF ENGINEER
SMK

BRANCH MANAGER
SMK

PM/DM
KKK

SATISFACTORY TO DATE
31 DEC 2025

ACTIVITY
AFMISC APPROVAL PER NAVFAC SAT-TO CHECKLIST

FOR COMMANDER NAVFAC
DATE 04/10/2026

APPROVED
[Signature]
DATE 04/10/2026

A/E INFO
JACOBSBURN A JOINT VENTURE
1100 NORTH GLEBE ROAD
SUITE 500
ARLINGTON, VA 22201
A/E Contract No. N62762-23-D-0002
A/E Task Order No. N62762-23-D-0010
A/E Task Order No. N62762-23-D-0011

SEAL
3/10/2026
JENNIFER M. HAYNES
90167
LICENSED PROFESSIONAL ENGINEER
STATE OF TEXAS

10-MAR-26
DATE

10-MAR-26
REVISED FHS

10-MAR-26
SYM DESCRIPTION

IF SHEET IS LESS THAN 22" X 34"
REDUCED PRINT. USE GRAPHIC SCALES


FILE NAME: C:\Users\Alfa\Documents\PO12-166555-A-3D_AlfacM.rvt
LAYOUT NAME: DETACHED EQUIPMENT YARD
PLOTED: 3/16/2026 4:25:08 PM
USER: CAA

D


C

B


A

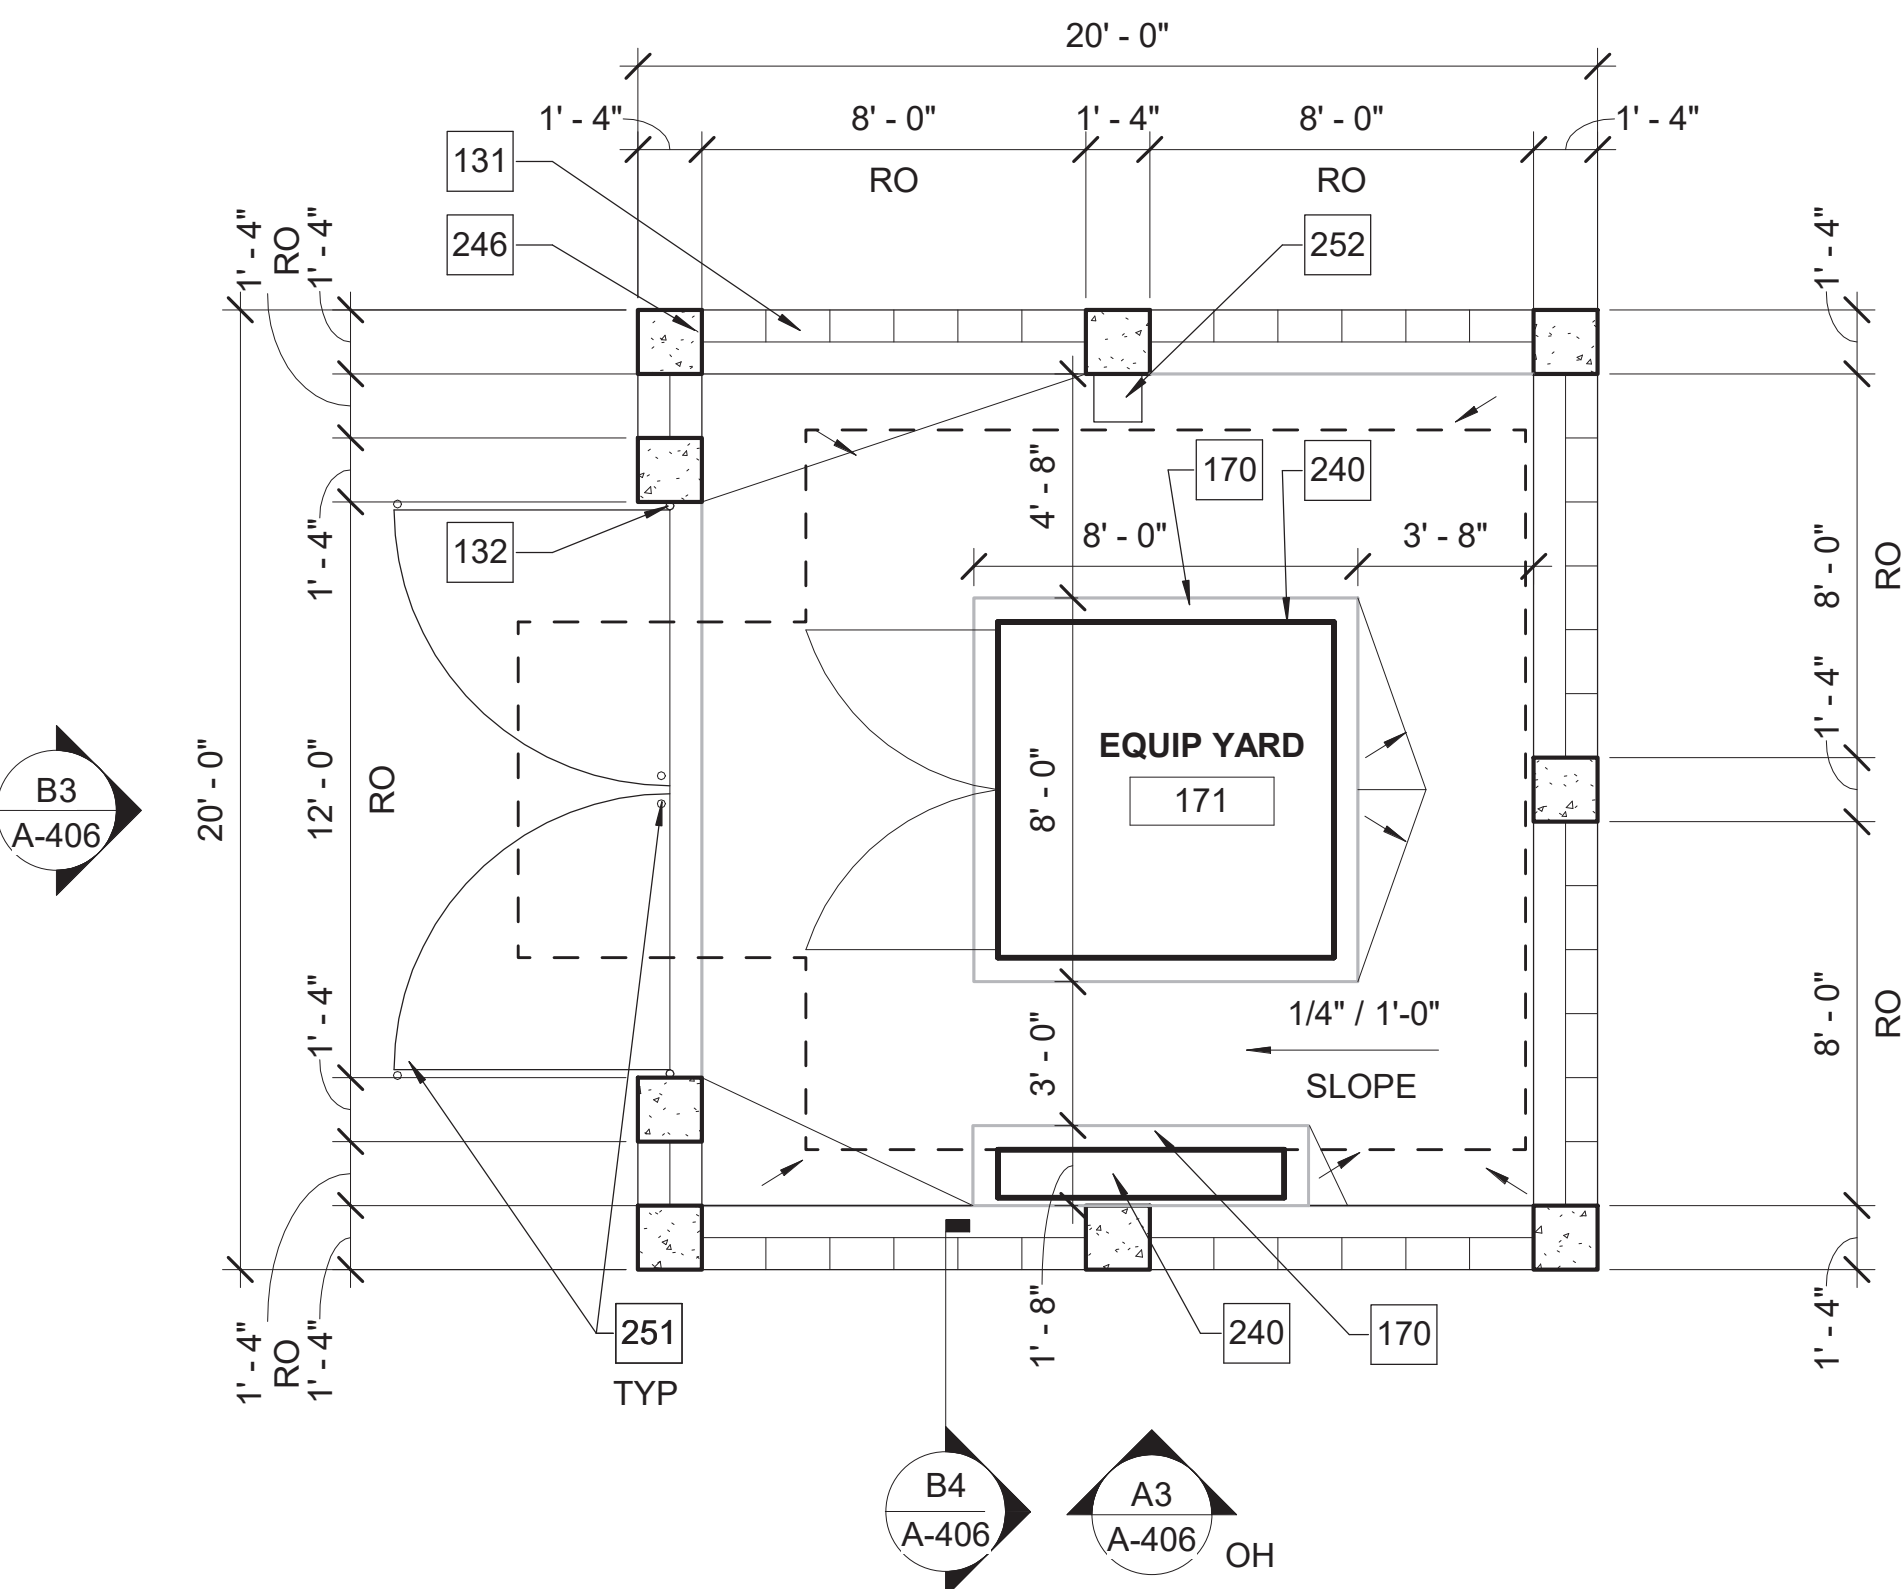

A1 EQUIPMENT YARD - ENLARGED PLAN
SCALE 1/4" = 1'-0"

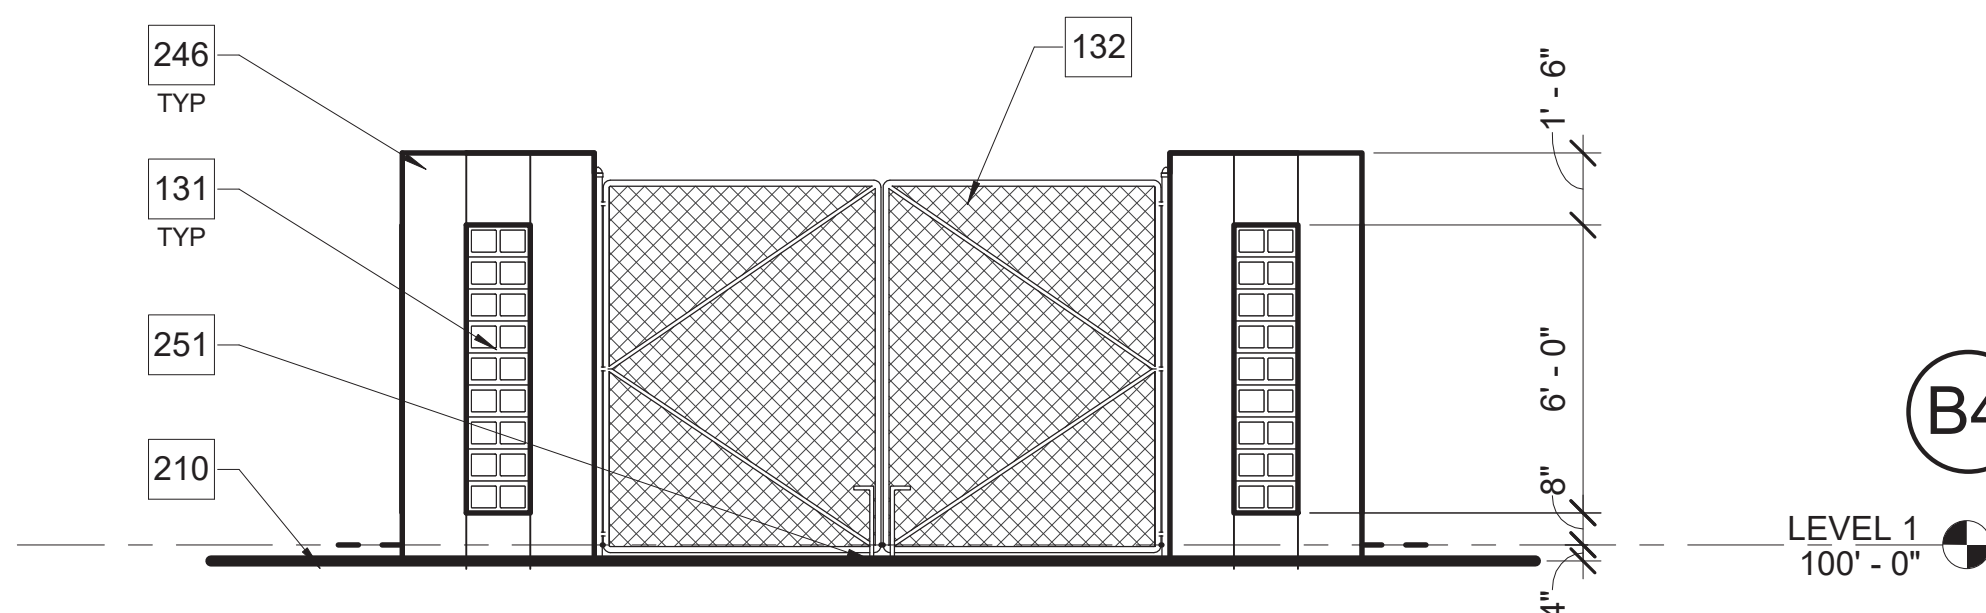


B3 EQUIPMENT YARD - FRONT ELEVATION
SCALE 1/4" = 1'-0"

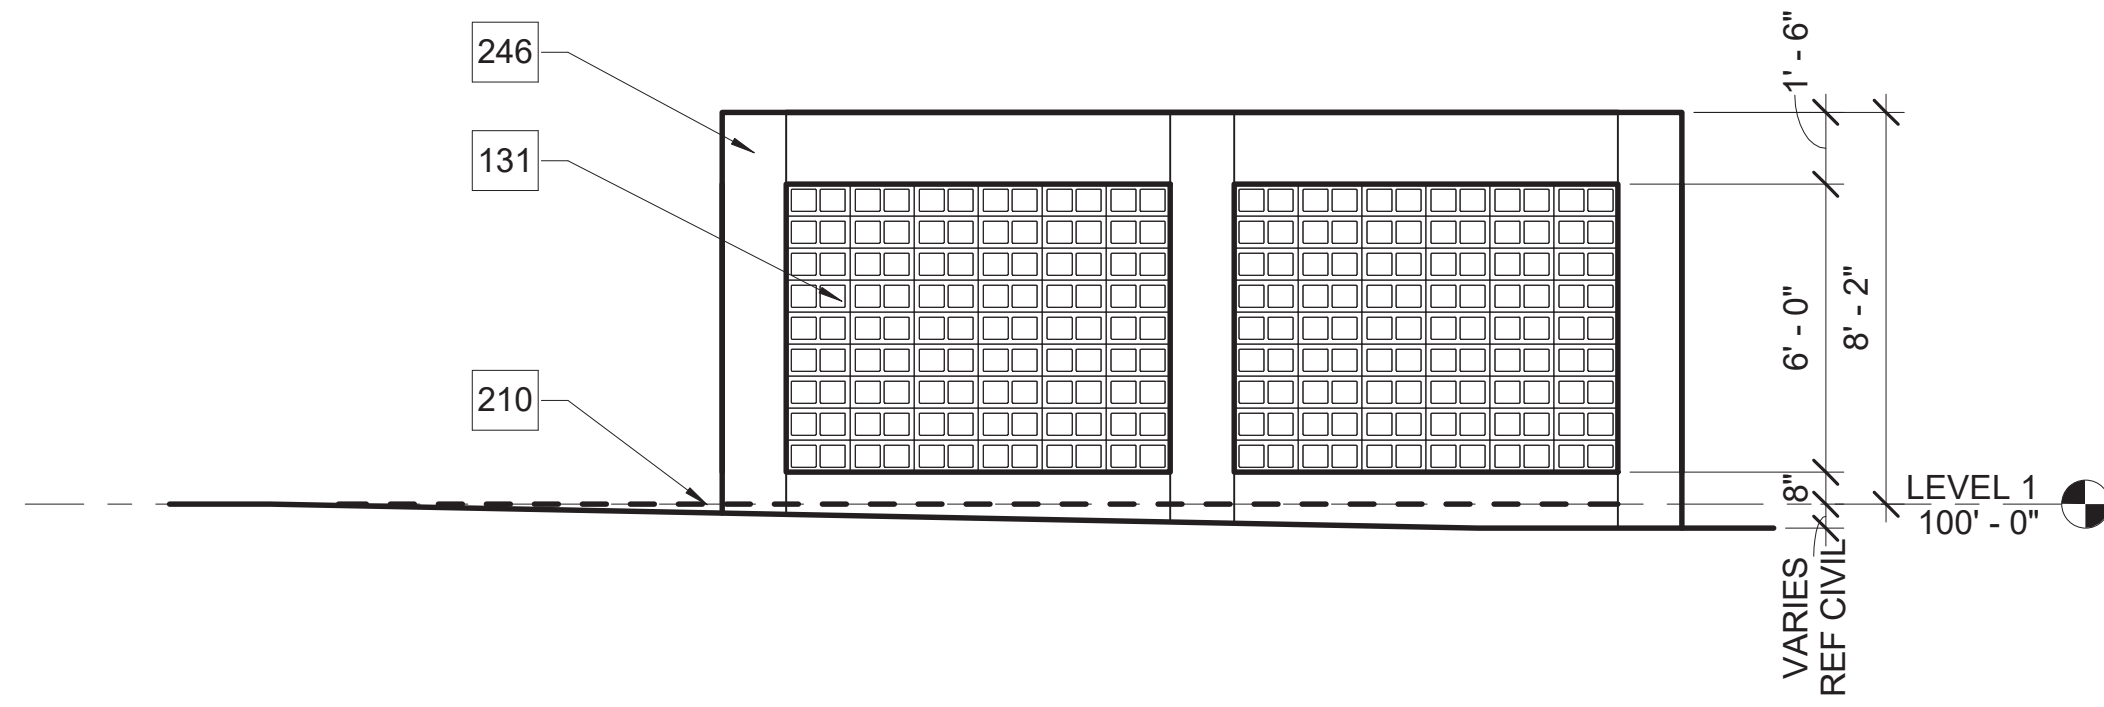



A3 EQUIPMENT YARD - SIDE ELEVATION
SCALE 1/4" = 1'-0"

EXTERIOR FINISH COLOR SCHEDULE			
ITEM CODE	REFERENCE COLOR	PAINT CODE	LOCATION
EX-1	ANTIQUE LINEN	23578	EXTERIOR CONCRETE WALLS, CMU BLOCKS
EX-3	TOBACCO BROWN	20117	GATE, MATCH SITE FENCING
NOTE: COORDINATE FINAL COLOR SELECTIONS WITH CONTRACTING OFFICER			

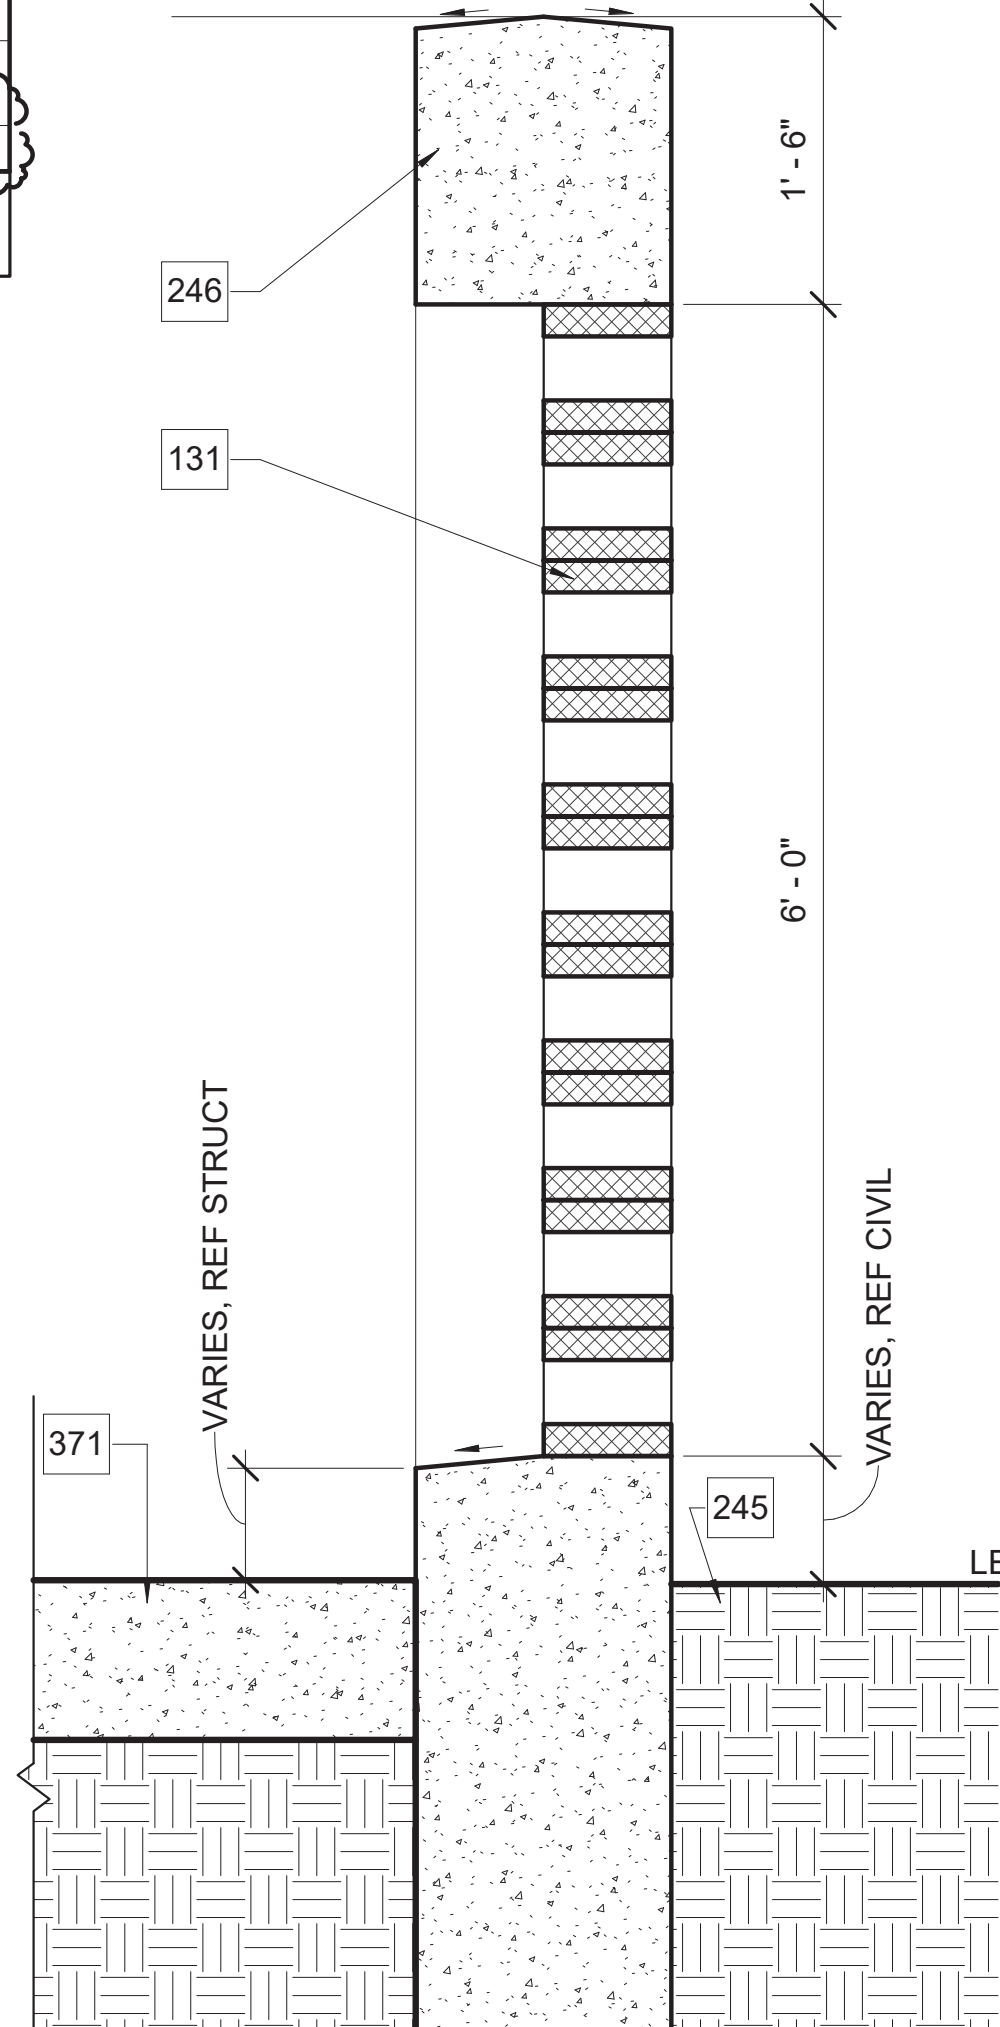

B4 WALL SECTION
SCALE NTS

KEYNOTES	
131	SIDE TURNED CMU BLOCK BREEZEWAY WITH FLUID APPLIED SILICONE ELASTOMERIC COATING (EX-1)
132	12'-0"W X 8'-0"H GALVANIZED AND PAINTED CHAIN LINK GATE, REFER TO FENCING SPECIFICATION, PROVIDE PADLOCK AND COORDINATE KEYING WITH CONTRACTING OFFICER
170	REINFORCED CONCRETE HOUSEKEEPING PAD, COORDINATE FINAL LAYOUT WITH SELECTED EQUIPMENT; REFER A3/S-502
210	FINISH GRADE/PAVEMENT; REFER CIVIL
240	ELECTRICAL SITE EQUIPMENT, REFER ELECTRICAL, CIVIL
245	FINISH GRADE/PAVEMENT; REFER CIVIL
246	CAST IN PLACE CONC WALL WITH FLUID APPLIED SILICONE ELASTOMERIC COATING, (EX-1), REFER STRUCTURAL
251	CORE 1" DIA, 1" DEEP HOLES INTO CONCRETE AT OPEN AND CLOSED LOCATIONS FOR 5/8" DIA GALVANIZED STEEL FOOT BOLTS WITH (2) 3/16" WALL BUSHINGS
252	WALL MOUNTED KILOWATT METER 12"x12", REFER TO ELECTRICAL
371	REINFORCED CONCRETE SLAB AND FOUNDATION, REFER STRUCTURAL

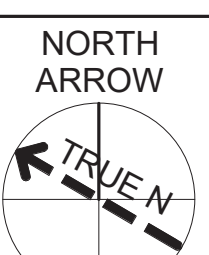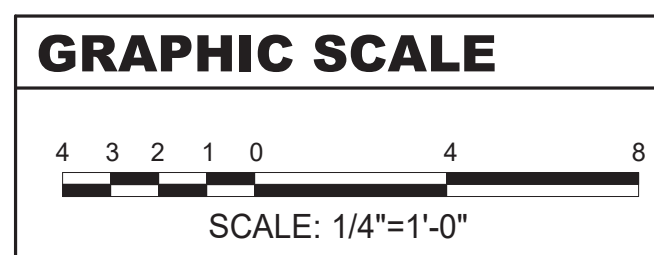

16-MAR-26	DATE
2	ADD CMU COATING, UPDATE GATE COLOR
SYM	DESCRIPTION

NAVFAC

REGISTERED ARCHITECT
CHRIS ALFARO
STATE OF TEXAS
26963

JACOBS / BURNS MEDONNELL

JACOBS&BAM, A JOINT VENTURE
1100 NORTH GLEBE ROAD
SUITE 500
ARLINGTON, VA 22201
AE Contract No. NA74524-0-0000
AE Task Order No. NA74524-0-0001
AE Task Order No. NA74524-0-0002

APPROVED
Chris Alfaro
FOR COMMANDER NAVFAC DATE 04/10/2026

ACTIVITY
AFMISC APPROVAL PER NAVFAC SAT-TO CHECKLIST

SATISFACTORY TO DATE 31 DEC 2026

DES: CAA DRW: CAA REV: MH
PM/DM KKK
BRANCH MANAGER SMK
CHIEF ENG/ARCH SMK
FIRE PROTECTION RO

DEPARTMENT OF THE NAVY
NAVAL FACILITIES ENGINEERING SYSTEMS COMMAND
NAVFAC PACIFIC
ANDERSEN AIR FORCE BASE

JOINT REGION MARIANAS (JRM)
GUAM

FY24 AJY183012 (P-012).
PDI: NORTH AIRCRAFT PARKING RAMP
DETACHED EQUIPMENT YARD

SCALE: AS SHOWN
EPROJETS NO.: 1665555
CONSTR CONTROL NO.

NAVFAC DRAWING NO.
17361884

SHEET 251 OF 377

A-406

REDESIGN FINAL SUBMITTAL

IF SHEET IS LESS THAN 22" X 34"
REDUCED PRINT. USE GRAPHIC SCALES

FILE NAME: C:\Revit_P\Projects\133097_E_Central_bdpinkley@burnsmcd.com.rvt
LAYOUT NAME: ELECTRICAL SITE DETAILS
PLOTTED: 3/10/2026 2:53:42 PM
USER: BDP

D


C

B

A

GENERAL NOTES:

- A. PROVIDE #3 REBAR CAGE IN DUCTBANK WHERE THE DUCTBANK IS INSTATED UNDER ROADWAYS.

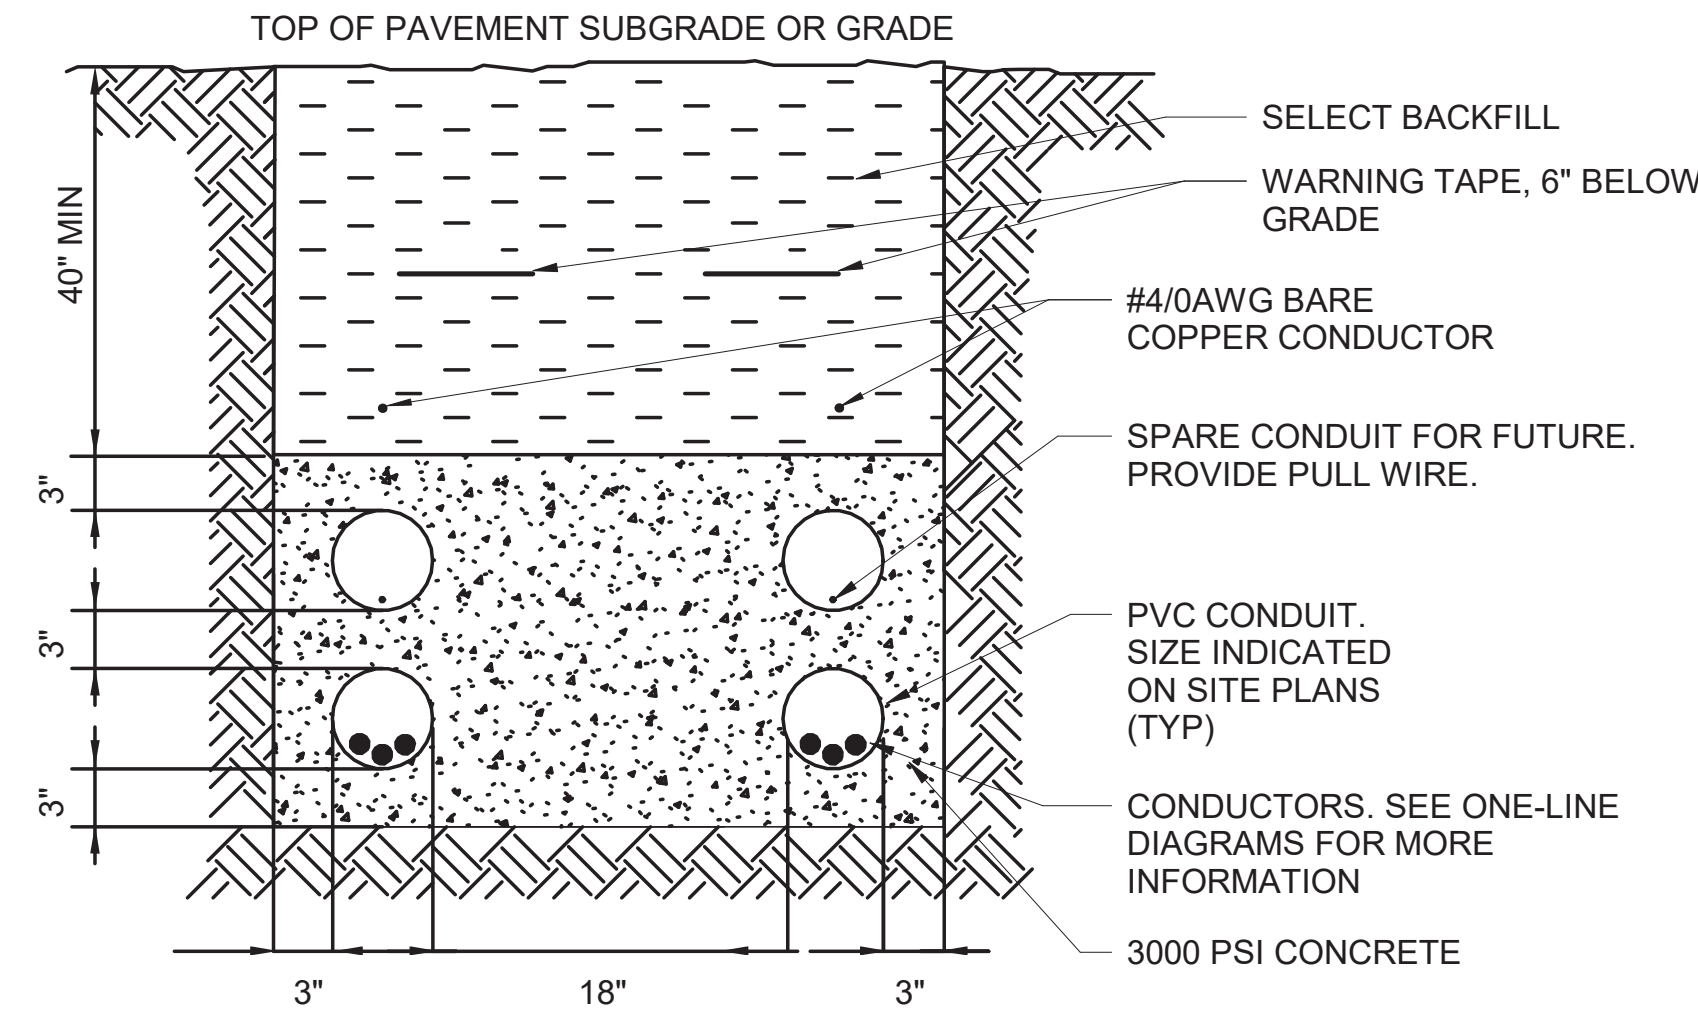


NOTES:

1. USE PLASTIC CONDUIT SPACERS AT 5'-0" OC.
2. THE #4/0 BARE COPPER CONDUCTOR SHOWN ABOVE THE CONCRETE ENCASED DUCTBANK IS IN ADDITION TO THE GROUND CONDUCTOR INDICATED ON THE ONE-LINE DIAGRAM SHOWN ON DRAWING EP601.

C4 2-WAY CONCRETE ENCASED DUCTBANK

SCALE: NTS

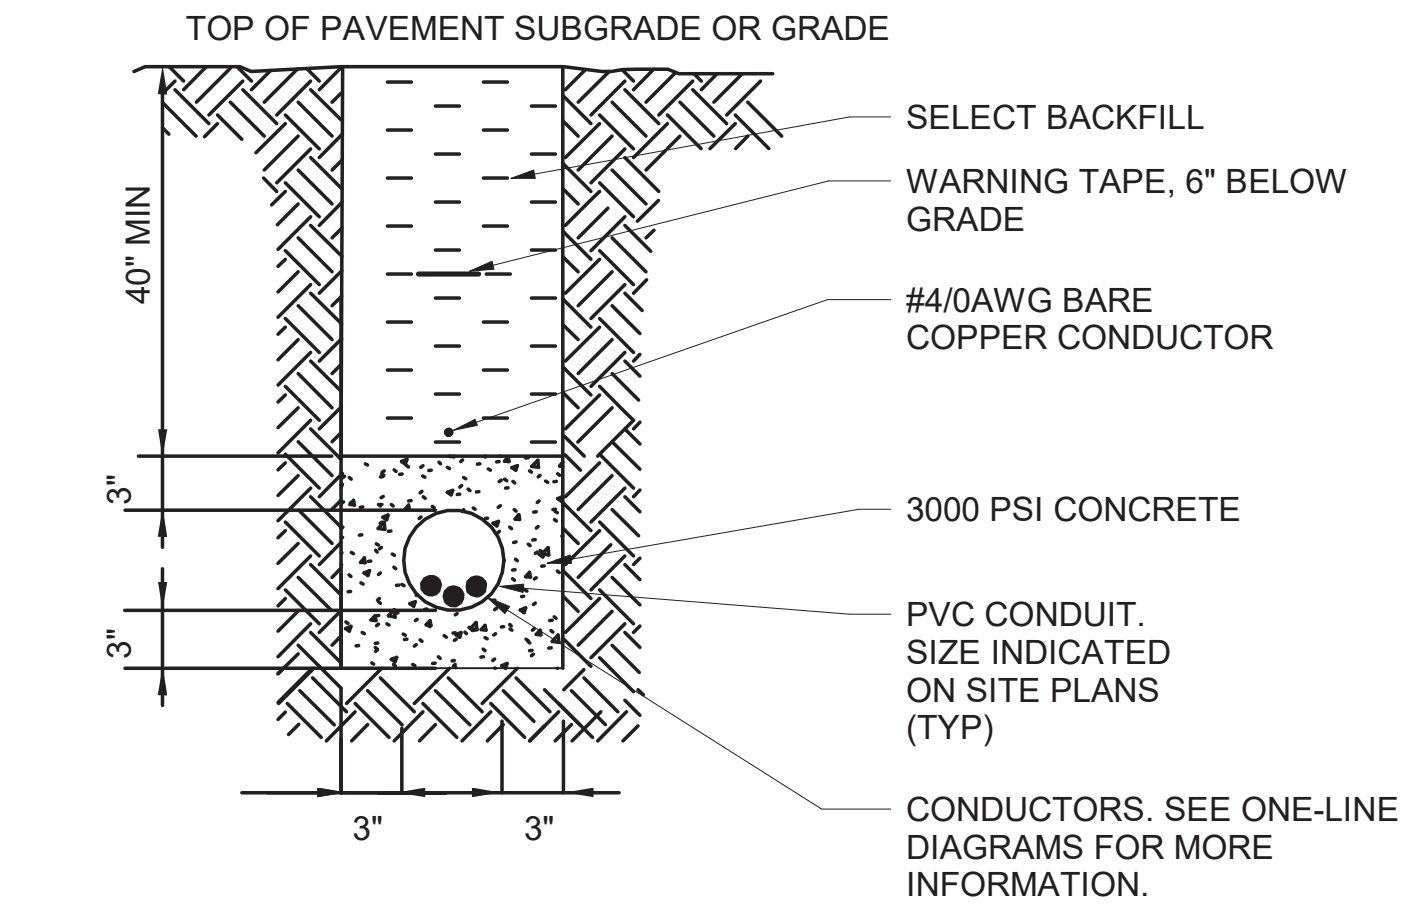


NOTES:

1. USE PLASTIC CONDUIT SPACERS AT 5'-0" OC.
2. THE #4/0 BARE COPPER CONDUCTOR SHOWN ABOVE THE CONCRETE ENCASED DUCTBANK IS IN ADDITION TO THE GROUND CONDUCTOR INDICATED ON THE ONE-LINE DIAGRAM SHOWN ON DRAWING EP601.

A4 1-WAY CONCRETE ENCASED DUCTBANK

SCALE: NTS

SYMBOL	DESCRIPTION	DATE
1	AMEND 003 - UPDATED GROUNDING REQUIREMENTS	10-MAR-26

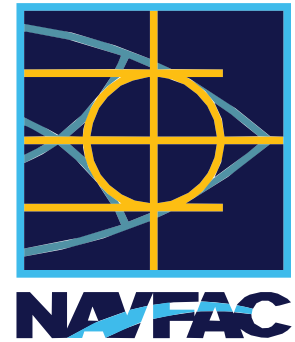

SEAL

Jacobs / BURNS MEDONNELL
JACOBS&B&M, A JOINT VENTURE
1100 NORTH GLEBE ROAD
SUITE 500
ARLINGTON, VA 22201
A/E Contract No. N6742-20-D-0002
A/E Title: Civil, Mech, Electrical, P&ID

A/E INFO

APPROVED
FOR COMMANDER NAVFAC DATE 04/10/2026

ACTIVITY
AFMISC APPROVAL PER NAVFAC
SAT-TO CHECKLIST

SATISFACTORY TO DATE 31 DEC 2025

DES:	DSB	DRW:	BDP	REV:	SDS
PM/DM					KKK
BRANCH MANAGER					SMK
CHIEF ENG/ARCH					SMK
FIRE PROTECTION					RO

DEPARTMENT OF THE NAVY
NAVFAC PACIFIC
ANDERSEN AIR FORCE BASE

NAVAL FACILITIES ENGINEERING SYSTEMS COMMAND
NAVAL FACILITIES ENGINEERING SYSTEMS COMMAND - PACIFIC
JOINT REGION MARIANAS (JRM)
GUAM

FY24 AJJY183012 (P-012),
PDI: NORTH AIRCRAFT PARKING RAMP
ELECTRICAL SITE DETAILS

SCALE: AS SHOWN
EPROJECTS NO.: 1665555
CONSTR CONTROL NO.
NAVFAC DRAWING NO. 17361899
SHEET 276 OF 377
ES504

IF SHEET IS LESS THAN 22" X 34"
REDUCED PRINT. USE GRAPHIC SCALES

REDESIGN FINAL SUBMITTAL

D

C

B

A

D

C

B


A

GENERAL NOTES

A. ITEMS SHOWN UNDER THE BOLD HATCH ON THIS SHEET INDICATE DEMOLITION SCOPE. OTHER ITEMS REPRESENT EXISTING CONDITIONS.

KEYED NOTES

001. PROVIDE 1- 6" CONDUIT WITH 3-500 KCMIL, CU, 15KV CABLE AND 1-#4/0 GROUND FROM EXISTING SWITCH ST16-5 TO EXISTING SWITCH SW-16-11; 1 -6" SPARE CONDUIT
002. PROVIDE 1- 6" CONDUIT WITH 3-500 KCMIL, CU, 15KV CABLE AND 1-#4/0 GROUND FROM EXISTING SWITCH ST16-6 TO EXISTING SWITCH SW-16-11; 1 -6" SPARE CONDUIT
003. PROVIDE 75KVA 13.8KV-480/277V PADMOUNT TRANSFORMER. REFER TO SHEET ES103 FOR MORE INFORMATION.
004. PROVIDE 1-5" CONDUIT WITH 3- #4/0 AWG CU, 15KV CABLE AND 1-#4/0 GROUND FROM EXISTING SWITCH TO 75KV TRANSFORMER. 1-5" SPARE CONDUIT.

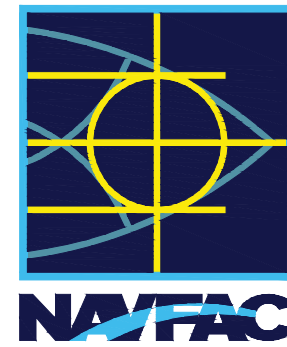

JACOBS BURNS & MCDONNELL
JACOBSBURN, A JOINT VENTURE
1100 NORTH GLEBE ROAD
SUITE 500
ARLINGTON, VA 22201

A/E Contract No. N62103-20-D-0002
A/E Task Order No. N62103-20-D-0002
A/E No. 2045002

APPROVED
Steven D. Stratton
FOR COMMANDER NAVFAC DATE: 10/10/2026

ACTIVITY
AFIMSC APPROVAL PER NAVFAC SAT-TO CHECKLIST

SATISFACTORY TO DATE 31 DEC 2025

DES: DSB DRW: DSB REV: SDS

PM/CM KKK

BRANCH MANAGER SMK

CHIEF ENGINEER SMK

FIRE PROTECTION RO

NAVAL FACILITIES ENGINEERING SYSTEMS COMMAND
NAVAL FACILITIES ENGINEERING SYSTEMS COMMAND - PACIFIC
JOINT REGION MARIANAS (JRM)

GUAMI

FY24 ALJY183012 (P-012).
PDI: NORTH AIRCRAFT PARKING RAMP

EXISTING DISTRIBUTION ONE LINE DIAGRAM - NEW WORK

REDESIGN FINAL SUBMITTAL

SCALE: AS SHOWN

PROJECTS NO.: 1665555

CONSTR CONTROL NO.

NAVFAC DRAWING NO. 17361903

SHEET 280 OF 377

EP601

A2 EXISTING DISTRIBUTION ONE LINE DIAGRAM - NEW WORK

SCALE: NTS

FILE NAME: \\bmcdburnsmcd.com\dfs\Clients\USNavy\Proc\133097_GuamP012NAR\Design\Elec\Sheets\TD101-TD102.dwg
LAYOUT NAME: TD101
PLOTTED: 03/10/2026 3:47pm
USER: bdpinkley

D

C


B

A


A1

TELECOMMUNICATIONS SITE DEMOLITION PLAN 1



SCALE: 1"= 80'

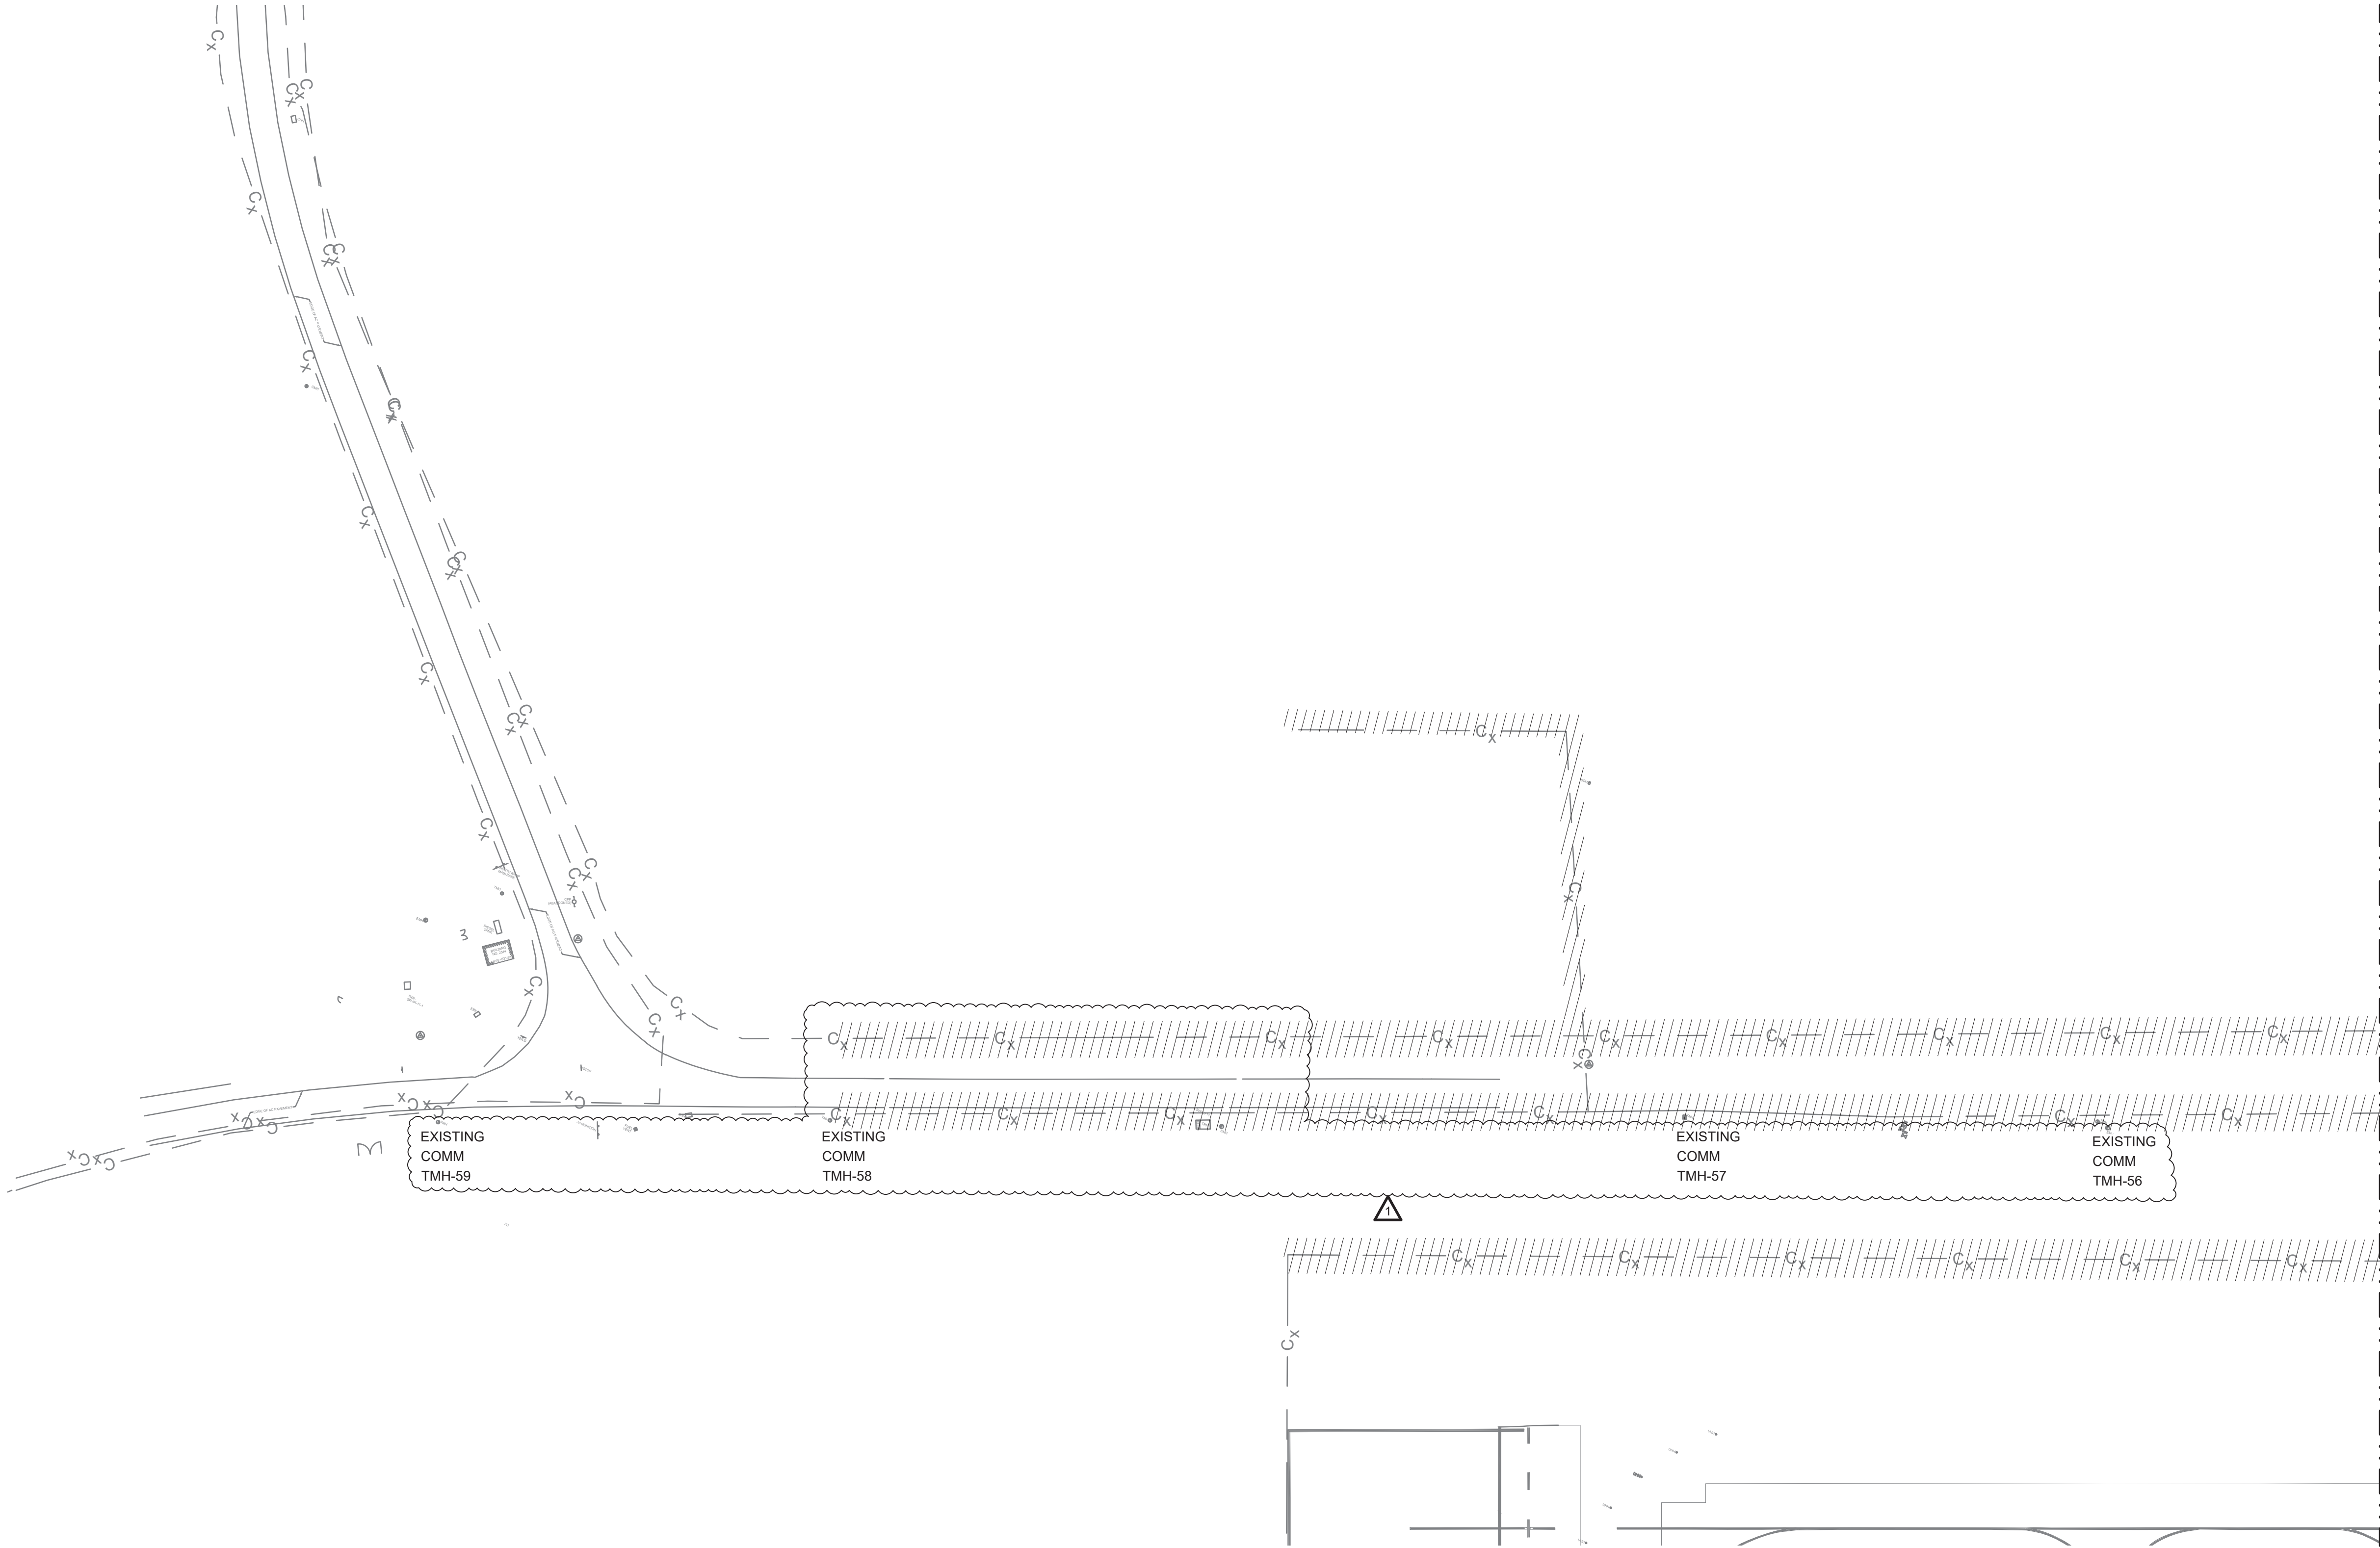

MATCHLINE, SEE TD102

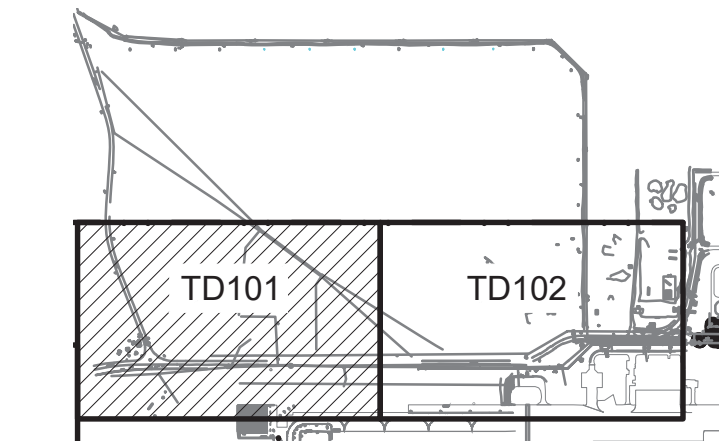

AREA KEY MAP

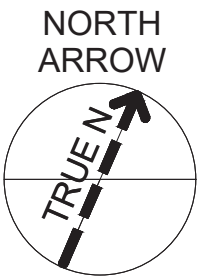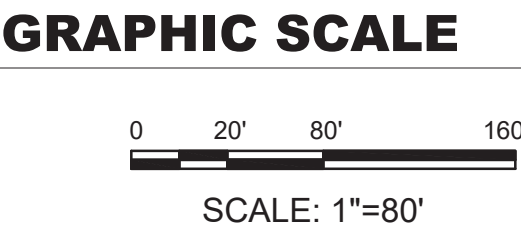

GENERAL NOTES - SITE PLANS

- A. THESE DRAWINGS ARE SUPPLEMENTAL TO THE PROJECT SPECIFICATIONS, ARE SCHEMATIC IN NATURE AND MUST NOT BE USED FOR FIELD INSTALLATION. FIELD INSTALLATION MUST BE IN ACCORDANCE WITH APPROVED SHOP DRAWINGS. SEE PROJECT SPECIFICATIONS FOR SHOP DRAWING REQUIREMENTS. THE LAYOUT OF TELECOMMUNICATIONS EQUIPMENT MUST BE FULLY COORDINATED WITH OTHER TRADES AND EQUIPMENT PRIOR TO SUBMISSION OF SHOP DRAWINGS FOR APPROVAL.
- B. SEE SHEET TS001 FOR PROJECT GENERAL NOTES, SYMBOL LEGEND AND ABBREVIATIONS.
- C. COORDINATE MAINTENANCE HOLE PLACEMENT SCHEDULE WITH CONTRACTING OFFICER SUCH THAT PLACEMENT CAN BE WITNESSED BY GOVERNMENT.
- D. COORDINATE DUCTBANK INSPECTION WITH CONTRACTING OFFICER SUCH THAT GOVERNMENT MAY INSPECT PRIOR TO POURING CONCRETE REINFORCEMENT.
- E. LOCATIONS OF MAINTENANCE HOLES AND DUCTBANKS ARE APPROXIMATE. CONFIRM THE LOCATION OF THE MAINTENANCE HOLES AND DUCTBANKS WITH THE CONTRACTING OFFICER. OBTAIN CONTRACTING OFFICER APPROVAL OF MAINTENANCE HOLE LOCATIONS AND ORIENTATION PRIOR TO THE COMMENCEMENT OF WORK.
- F. INFRASTRUCTURE MUST BE INSTALLED AND CUT OVER PRIOR TO DEMOLITION WORK. COORDINATE CUTOVER WITH COMMUNICATION SQUADRON.



Jacobs **BURNS & MCDONNELL**
JACOBSBAM, A JOINT VENTURE
1100 NORTH GLEBE ROAD
SUITE 500
ARLINGTON, VA 22201

APPROVED
FOR COMMANDER NAVFAC DATE 04/10/2026

ACTIVITY
AFMISC APPROVAL PER NAVFAC
SAT-TO CHECKLIST

SATISFACTORY TO DATE 31 DEC 2026

DES: TGB DRW: BDP REV: SDS

PMIDM KKK

BRANCH MANAGER SMK

CHIEF ENGINEER SMK

FIRE PROTECTION RO

DEPARTMENT OF THE NAVY
NAVFAC PACIFIC
ANDERSEN AIR FORCE BASE

NAVAL FACILITIES ENGINEERING SYSTEMS COMMAND
NAVAL FACILITIES ENGINEERING SYSTEMS COMMAND - PACIFIC
JOINT REGION MARIANAS (JRM)

GUAM

FY24 AJJY183012 (P-012)
PDI: NORTH AIRCRAFT PARKING RAMP
TELECOMMUNICATIONS SITE DEMOLITION PLAN 1

SCALE: AS SHOWN
EPROJECTS NO.: 1665555
CONSTR CONTROL NO.


NAVFAC DRAWING NO.
17361915

SHEET 202 OF 377

TD101


REDESIGN FINAL SUBMITTAL

FILE NAME: \\bmcdburnsmcd.com\dis\clients\USNavy\pac\133097_Guam\PO12NAR\Design\Elec\Sheets\PO12_1665555_TS101-TS105.dwg
LAYOUT NAME: TS101
PLOTTED: 03/10/2026 3:52pm
USER: bdpinkley

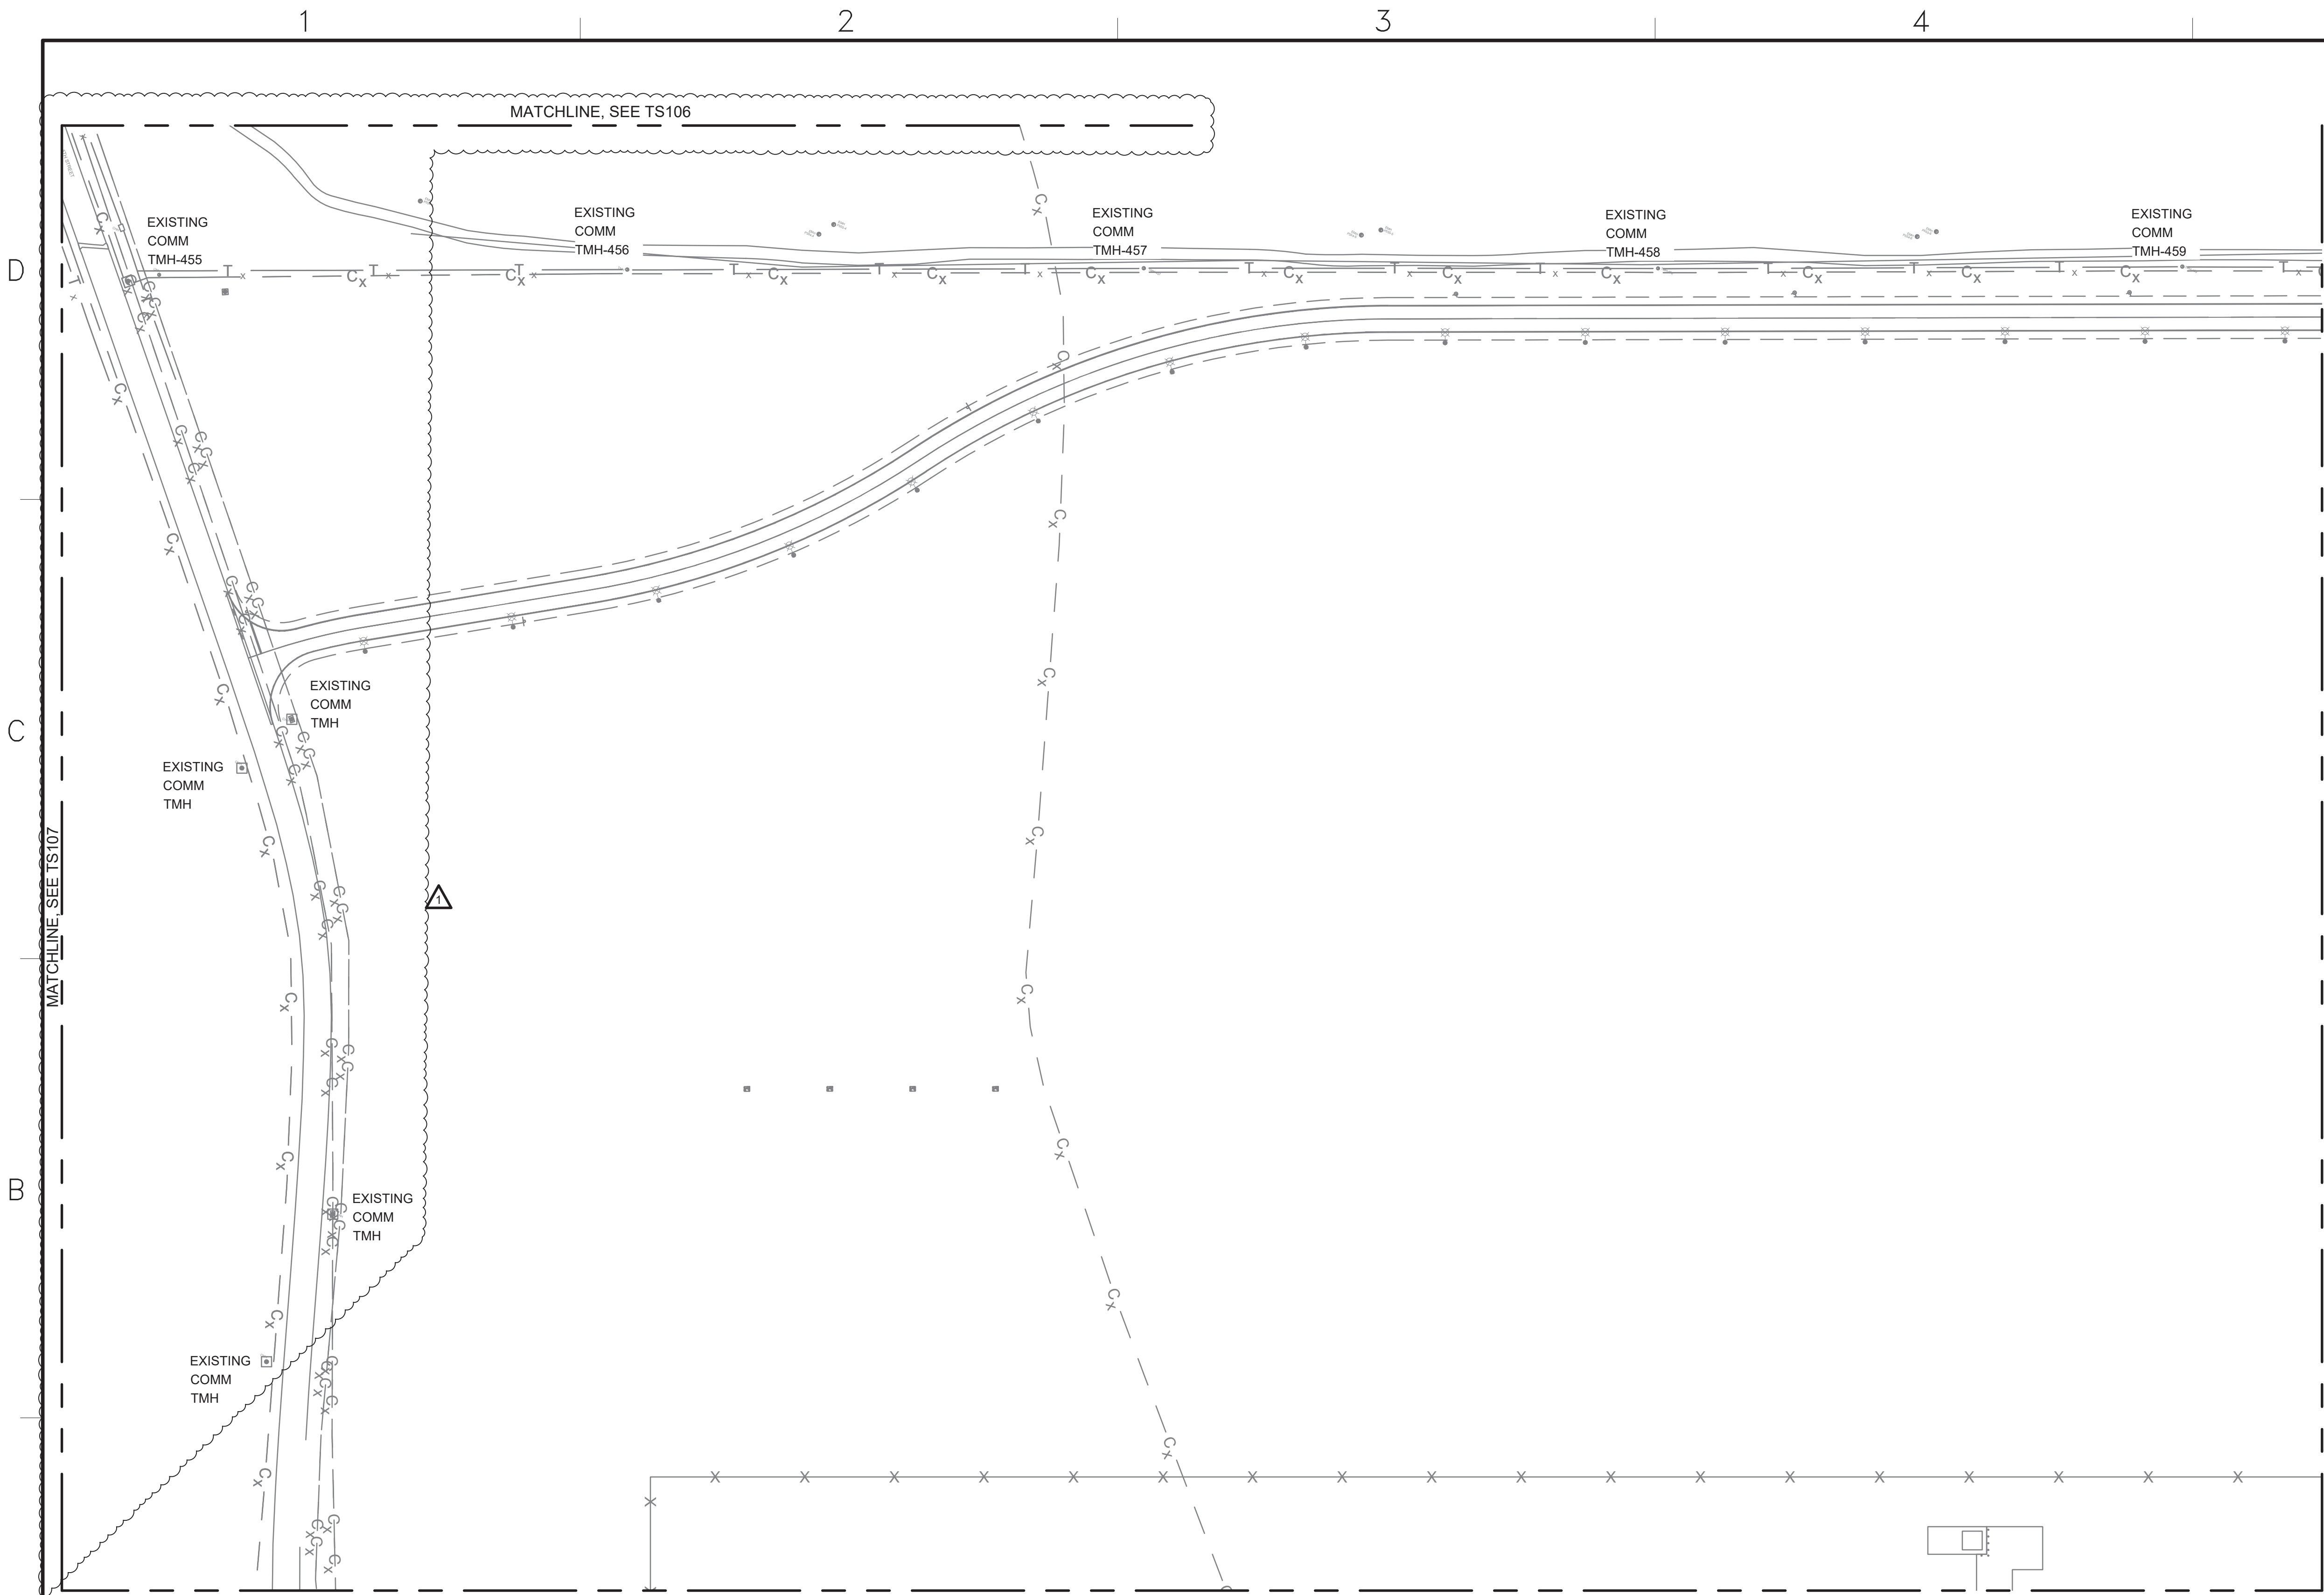

A1 TELECOMMUNICATIONS SITE PLAN 1
SCALE: 1" = 80'

- GENERAL NOTES - SITE PLANS**
- A. THESE DRAWINGS ARE SUPPLEMENTAL TO THE PROJECT SPECIFICATIONS, ARE SCHEMATIC IN NATURE AND MUST NOT BE USED FOR FIELD INSTALLATION. FIELD INSTALLATION MUST BE IN ACCORDANCE WITH APPROVED SHOP DRAWINGS. SEE PROJECT SPECIFICATIONS FOR SHOP DRAWING REQUIREMENTS. THE LAYOUT OF TELECOMMUNICATIONS EQUIPMENT MUST BE FULLY COORDINATED WITH OTHER TRADES AND EQUIPMENT PRIOR TO SUBMISSION OF SHOP DRAWINGS FOR APPROVAL.
 - B. SEE SHEET TS001 FOR PROJECT GENERAL NOTES, SYMBOL LEGEND AND ABBREVIATIONS.
 - C. COORDINATE MAINTENANCE HOLE PLACEMENT SCHEDULE WITH CONTRACTING OFFICER SUCH THAT PLACEMENT CAN BE WITNESSED BY GOVERNMENT.
 - D. COORDINATE DUCTBANK INSPECTION WITH CONTRACTING OFFICER SUCH THAT GOVERNMENT MAY INSPECT PRIOR TO POURING CONCRETE REINFORCEMENT.
 - E. LOCATIONS OF MAINTENANCE HOLES AND DUCTBANKS ARE APPROXIMATE. CONFIRM THE LOCATION OF THE MAINTENANCE HOLES AND DUCTBANKS WITH THE CONTRACTING OFFICER. OBTAIN CONTRACTING OFFICER APPROVAL OF MAINTENANCE HOLE LOCATIONS AND ORIENTATION PRIOR TO THE COMMENCEMENT OF WORK.
 - F. SEE SHEET TS701 TELECOMMUNICATIONS INTERBUILDING BACKBONE RISER FOR PROJECT CABLING REQUIREMENTS.

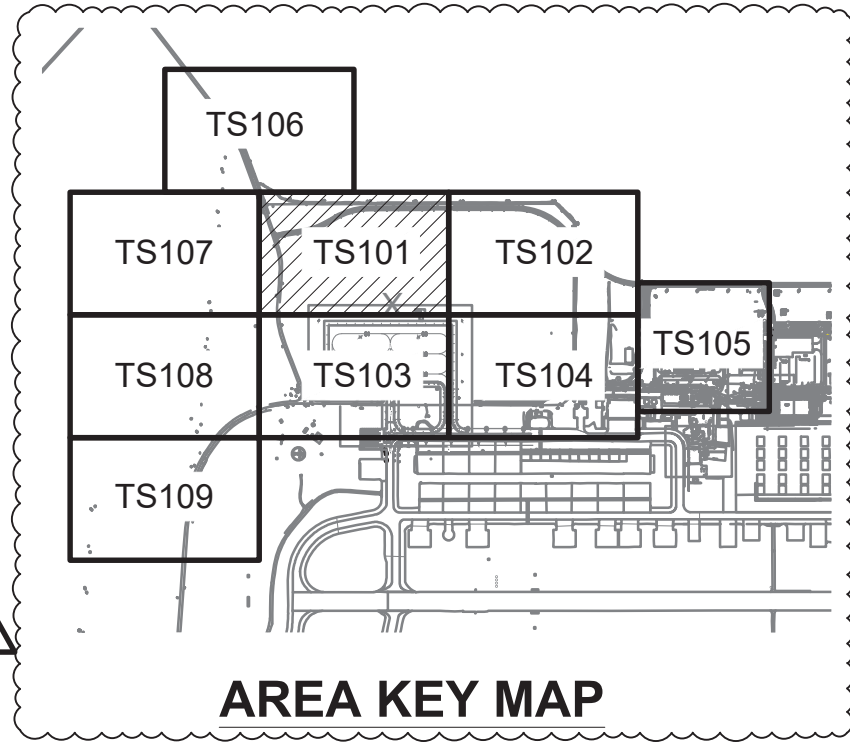


GRAPHIC SCALE
0 40' 80' 160'
SCALE: 1"=80'

NORTH ARROW
TRUE N




10-MAR-26 DATE	
1 AMEND.0002 - MH ID'S CHANGE SYM DESCRIPTION	
 JACOBSRAM, A JOINT VENTURE 1100 NORTH GLEBE ROAD SUITE 500 ARLINGTON, VA 22201 A/E Contract No. 1665555-20-0002 A/E Task Order No. 1665555-20-0002 A/E No. 2008024820 A/E INFO	
APPROVED FOR COMMANDER NAVFAC DATE 04/10/2026 ACTIVITY AFMISC APPROVAL PER NAVFAC SAT-TO CHECKLIST SATISFACTORY TO DATE 31 DEC 2026 DES: TOR DRW: BDP REV: SDS PMIDM KKK BRANCH MANAGER SMK CHIEF ENGINEER SMK FIRE PROTECTION RO	
DEPARTMENT OF THE NAVY NAVAL FACILITIES ENGINEERING SYSTEMS COMMAND NAVFAC PACIFIC ANDERSEN AIR FORCE BASE GUAM FY24 AUJY183012 (P-012) PDI: NORTH AIRCRAFT PARKING RAMP TELECOMMUNICATIONS SITE PLAN 1	
SCALE: AS SHOWN EPROJECTS NO.: 1665555 CONSTR CONTROL NO. NAVFAC DRAWING NO. 17361917 SHEET 204 OF 377 TS101	

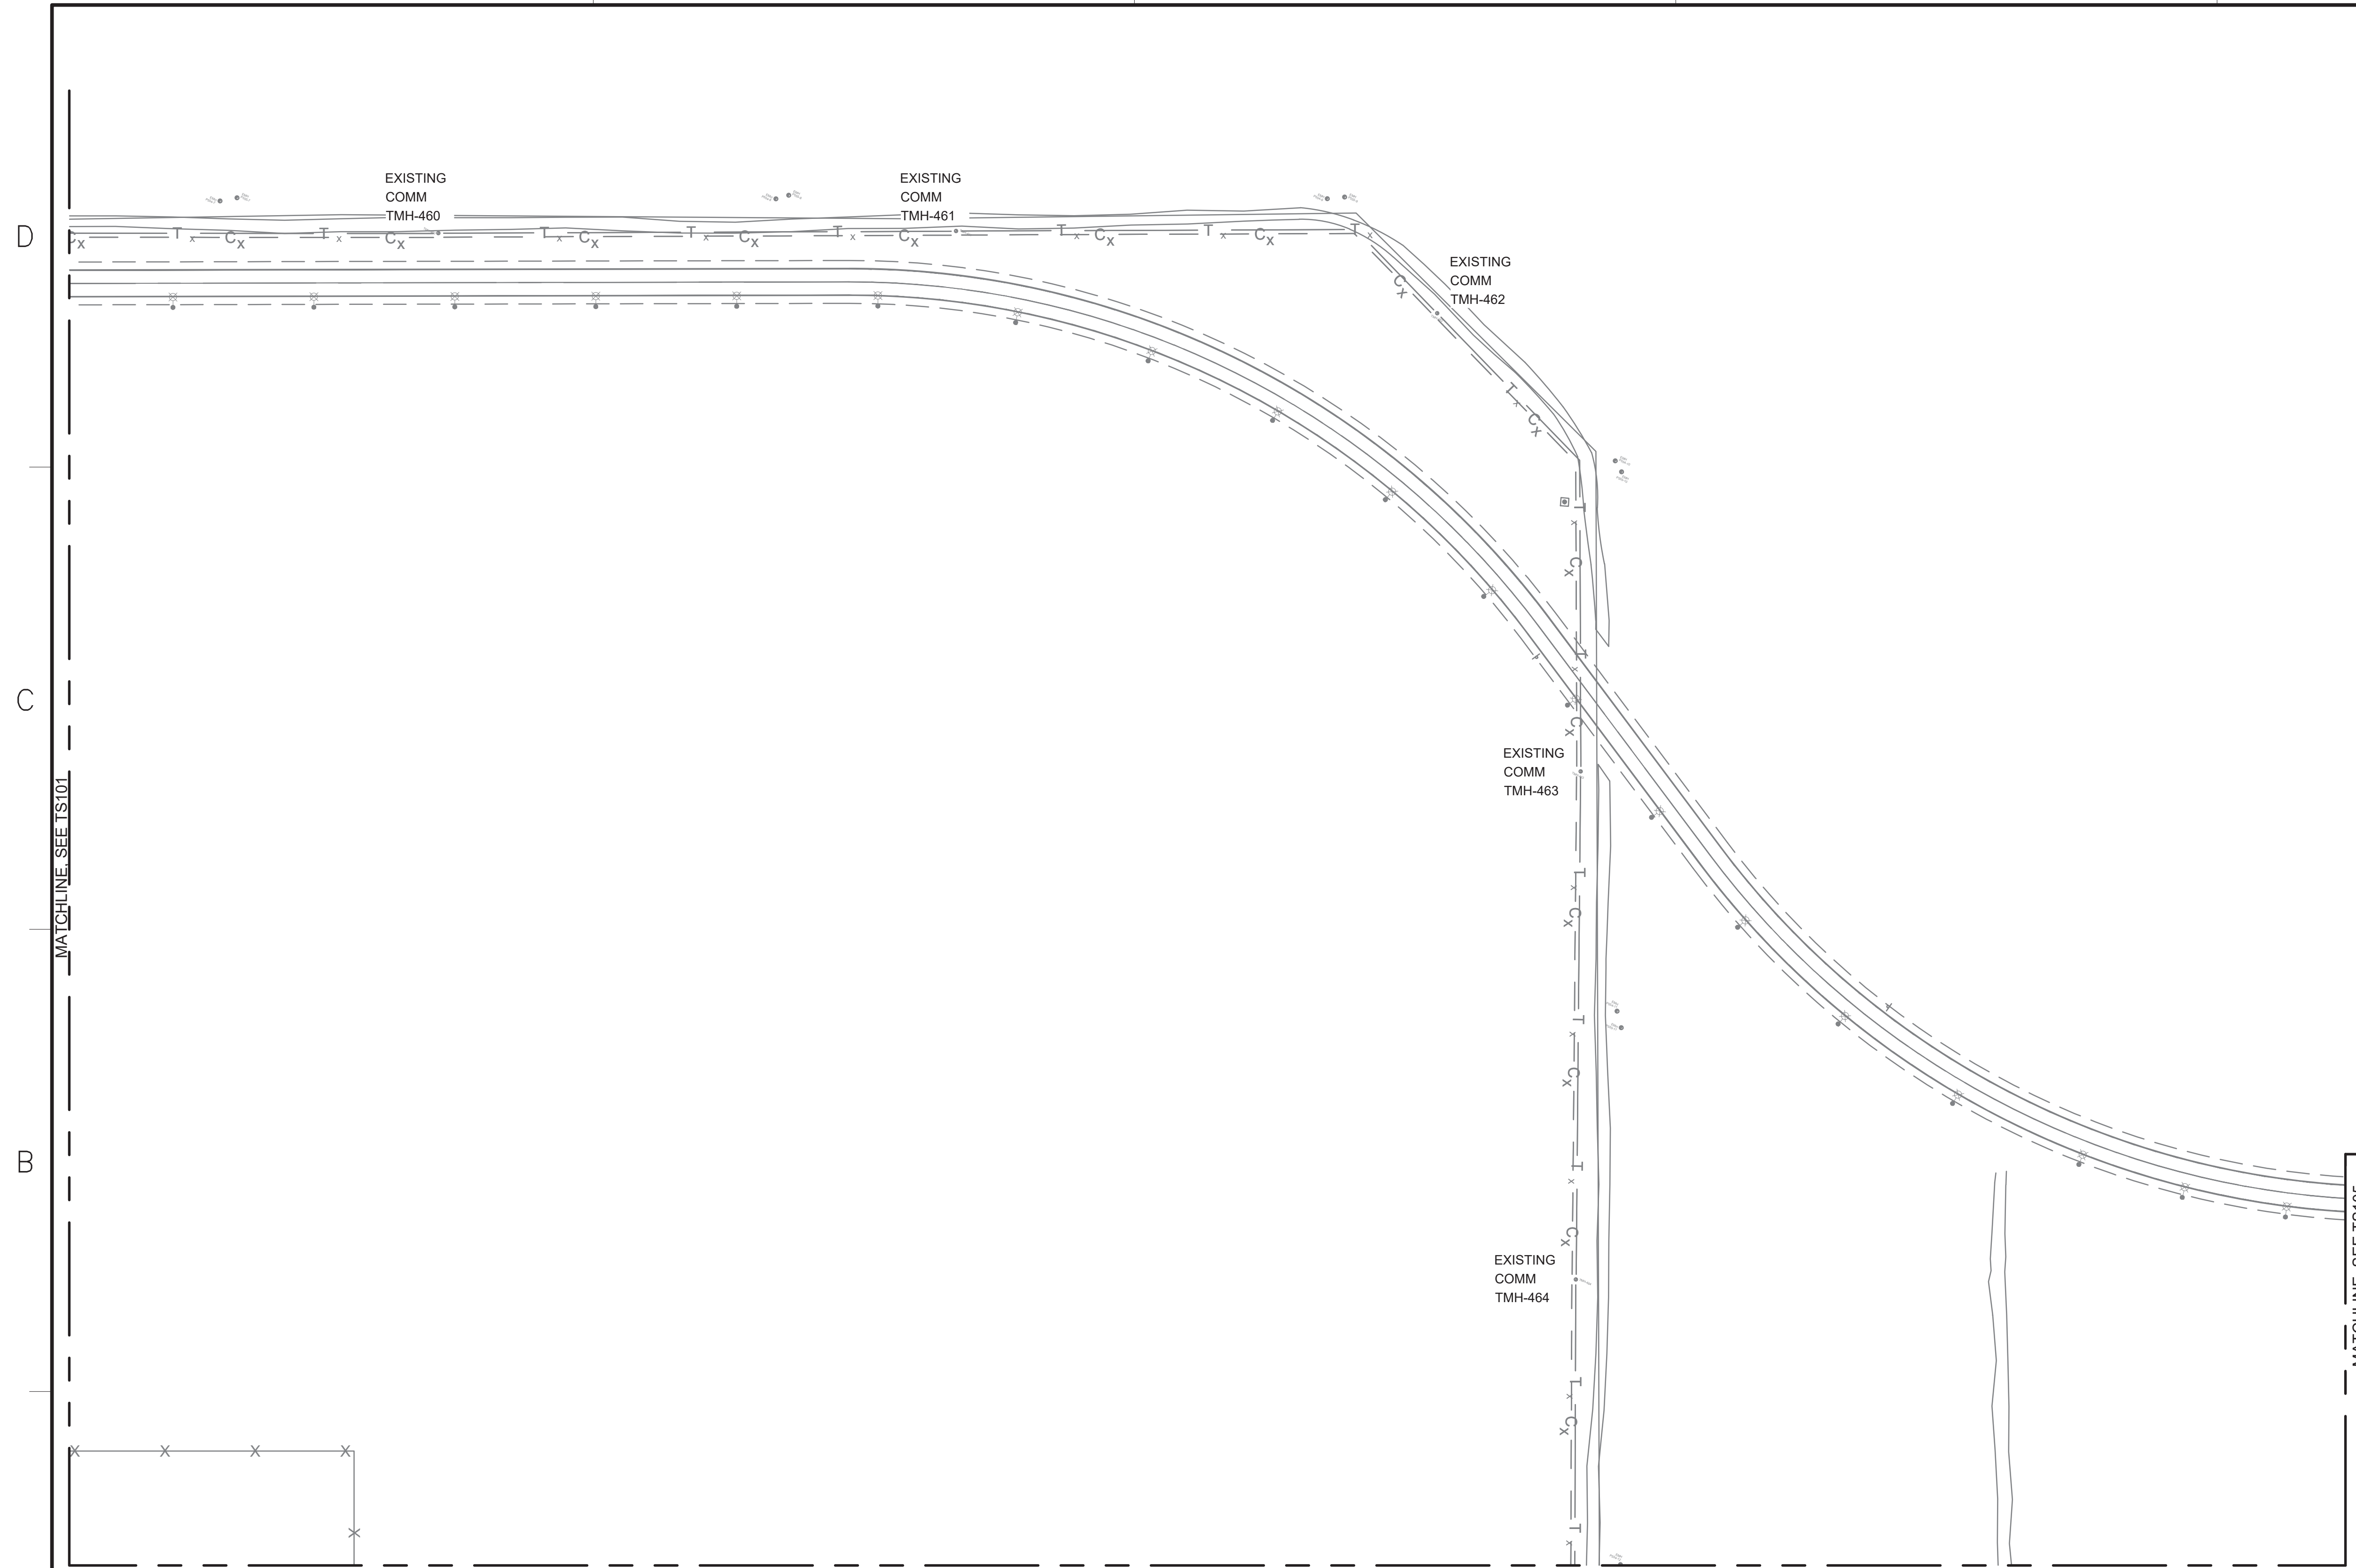

GENERAL NOTES - SITE PLANS

- | | |
|----|---|
| A. | THESE DRAWINGS ARE SUPPLEMENTAL TO THE PROJECT SPECIFICATIONS, ARE SCHEMATIC IN NATURE AND MUST NOT BE USED FOR FIELD INSTALLATION. FIELD INSTALLATION MUST BE IN ACCORDANCE WITH APPROVED SHOP DRAWINGS. SEE PROJECT SPECIFICATIONS FOR SHOP DRAWING REQUIREMENTS. THE LAYOUT OF TELECOMMUNICATIONS EQUIPMENT MUST BE FULLY COORDINATED WITH OTHER TRADES AND EQUIPMENT PRIOR TO SUBMISSION OF SHOP DRAWINGS FOR APPROVAL. |
| B. | SEE SHEET TS001 FOR PROJECT GENERAL NOTES, SYMBOL LEGEND AND ABBREVIATIONS. |
| C. | COORDINATE MAINTENANCE HOLE PLACEMENT SCHEDULE WITH CONTRACTING OFFICER SUCH THAT PLACEMENT CAN BE WITNESSED BY GOVERNMENT. |
| D. | COORDINATE DUCTBANK INSPECTION WITH CONTRACTING OFFICER SUCH THAT GOVERNMENT MAY INSPECT PRIOR TO POURING CONCRETE REINFORCEMENT. |
| E. | LOCATIONS OF MAINTENANCE HOLES AND DUCTBANKS ARE APPROXIMATE. CONFIRM THE LOCATION OF THE MAINTENANCE HOLES AND DUCTBANKS WITH THE CONTRACTING OFFICER. OBTAIN CONTRACTING OFFICER APPROVAL OF MAINTENANCE HOLE LOCATIONS AND ORIENTATION PRIOR TO THE COMMENCEMENT OF WORK. |
| F. | SEE SHEET TS701 TELECOMMUNICATIONS INTERBUILDING BACKBONE RISER FOR PROJECT CABLING REQUIREMENTS. |

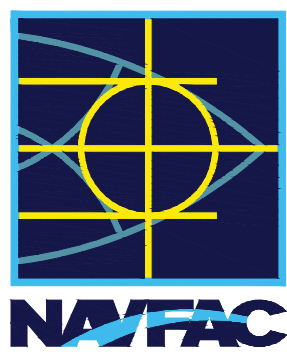

Jacobs / **BURNS & MCDONNELL**
JOBS/B&M, A JOINT VENTURE
10 NORTH GLEBE ROAD
SUITE 500
ARLINGTON, VA 22201

Task Order No. N6274221F0315
NO. D3430603

APPROVED

Mizum: 

COMMANDER NAVFAC DATE 04/10

NAVFA APPROVAL PER NAVFA
T-TO CHECKLIST

SFACTORY TO DATE		31 DEC	
TOP	BTM	DD	TTT

DRW: BDP	REV: S
----------	--------

FINCH MANAGER

EF ENG/ARCH

PROTECTION

M	M
-----	-----

GUA

ASIN: B000000000


IAN

FIC
MARCIF
INW

PA
GIO

MF

AND
INT

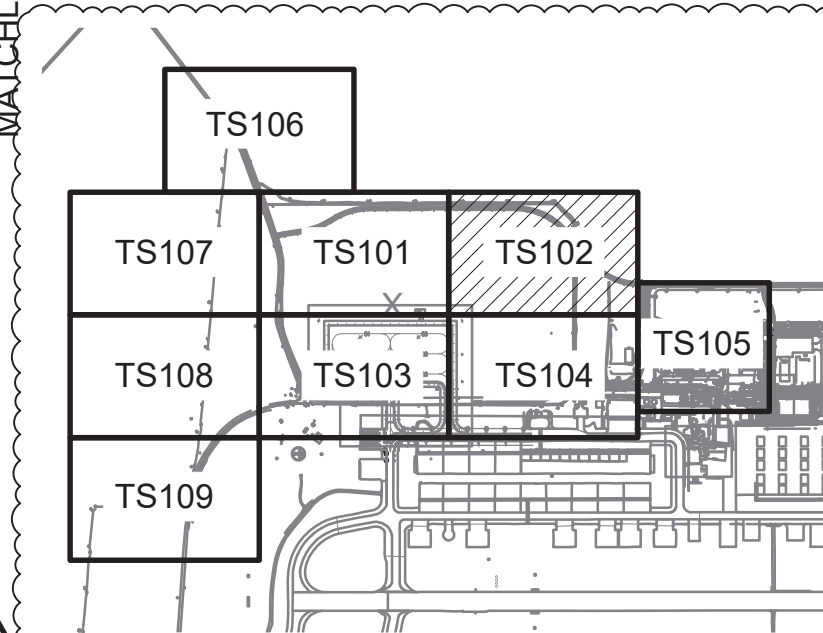


AREA KEY MAP

GRAPHIC SCALE



SCALE: 1"=80'

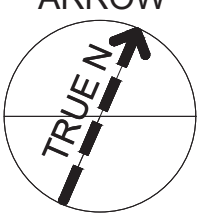NORTH
ARROW

AS SHOWN

PROJECTS NO.: 1665555

MASTER CONTROL NO.

FAC DRAWING NO.

17361918

ET 295 OF 377

TS102

IF SHEET IS LESS THAN 22" X 34"
REDUCED PRINT. USE GRAPHIC SCALES


FILE NAME: \\bmcdburnsmcd.com\dis\clients\USNavy\pac\133097_Guam\012NAR\Design\Elec\Sheets\012_1665555_TS101-TS105.dwg
LAYOUT NAME: TS104
PLOTTED: 03/10/2026 3:53pm
USER: bdpinkley

D

C

B

A

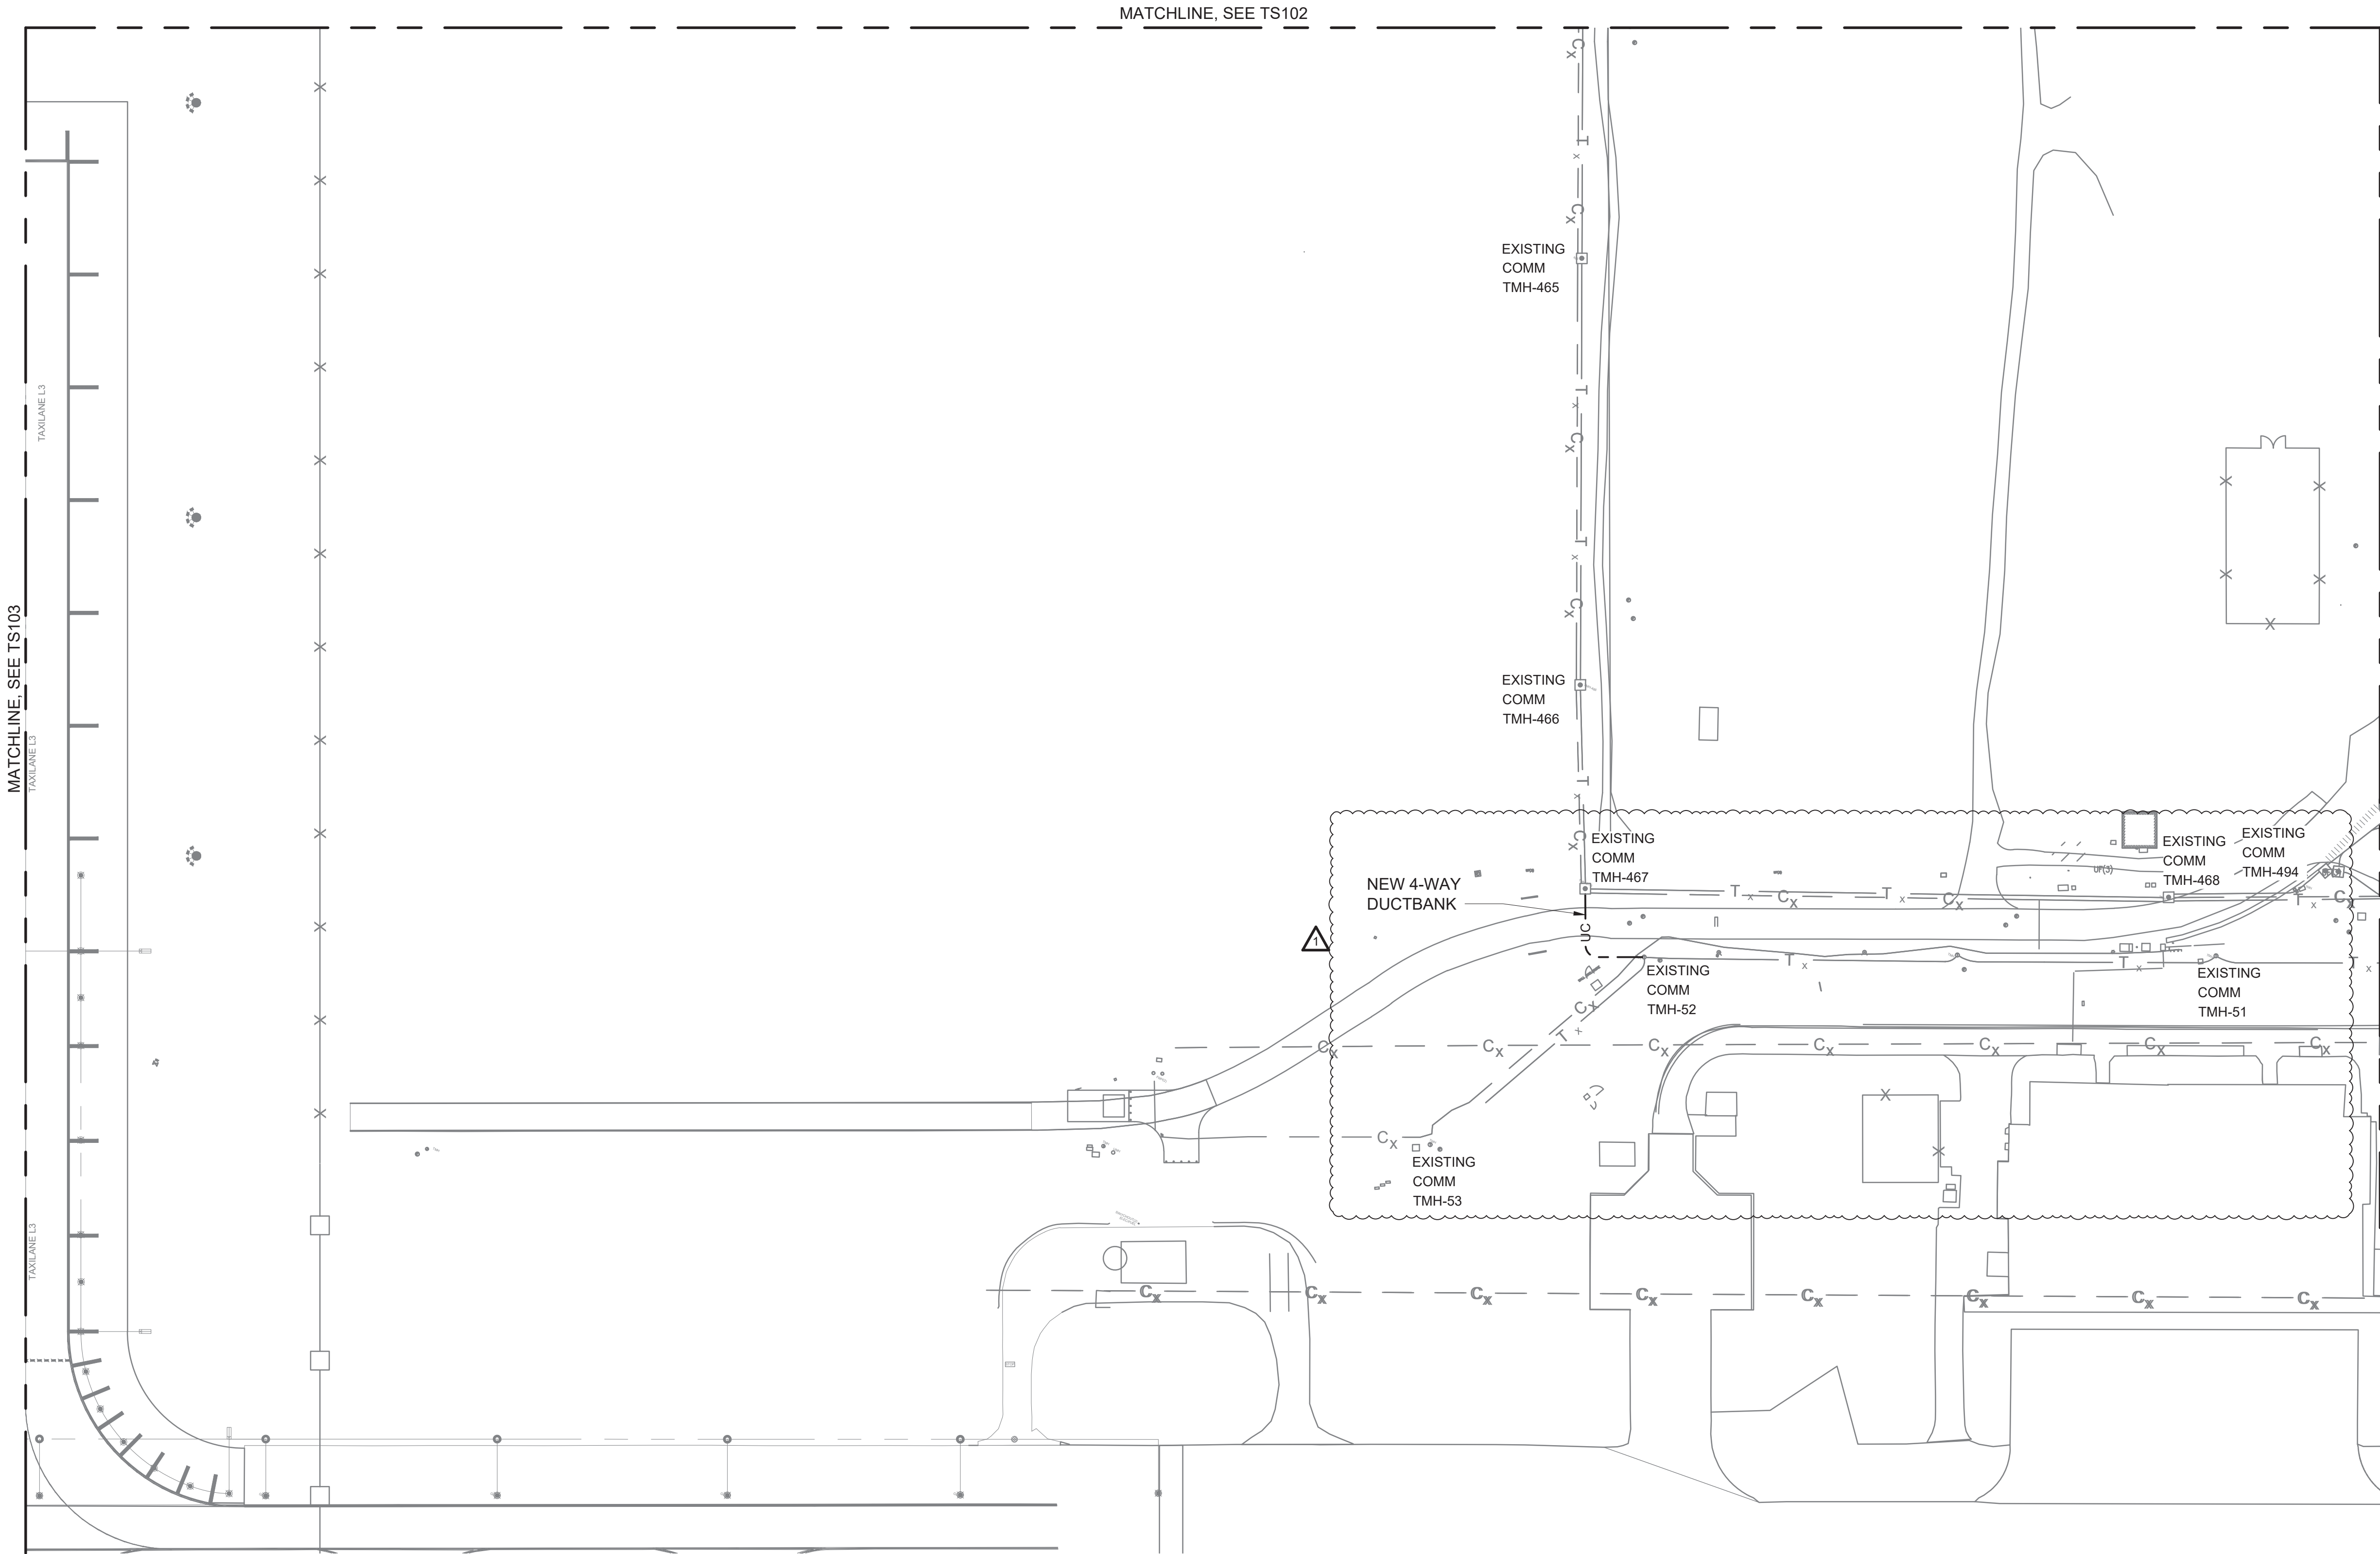

A1

TELECOMMUNICATIONS SITE PLAN 4

SCALE: 1" = 80'




GRAPHIC SCALE




SCALE: 1"=80'

NORTH ARROW

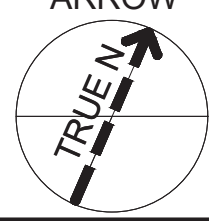

GENERAL NOTES - SITE PLANS

- A. THESE DRAWINGS ARE SUPPLEMENTAL TO THE PROJECT SPECIFICATIONS, ARE SCHEMATIC IN NATURE AND MUST NOT BE USED FOR FIELD INSTALLATION. FIELD INSTALLATION MUST BE IN ACCORDANCE WITH APPROVED SHOP DRAWINGS. SEE PROJECT SPECIFICATIONS FOR SHOP DRAWING REQUIREMENTS. THE LAYOUT OF TELECOMMUNICATIONS EQUIPMENT MUST BE FULLY COORDINATED WITH OTHER TRADES AND EQUIPMENT PRIOR TO SUBMISSION OF SHOP DRAWINGS FOR APPROVAL.
- B. SEE SHEET TS001 FOR PROJECT GENERAL NOTES, SYMBOL LEGEND AND ABBREVIATIONS.
- C. COORDINATE MAINTENANCE HOLE PLACEMENT SCHEDULE WITH CONTRACTING OFFICER SUCH THAT PLACEMENT CAN BE WITNESSED BY GOVERNMENT.
- D. COORDINATE DUCTBANK INSPECTION WITH CONTRACTING OFFICER SUCH THAT GOVERNMENT MAY INSPECT PRIOR TO POURING CONCRETE REINFORCEMENT.
- E. LOCATIONS OF MAINTENANCE HOLES AND DUCTBANKS ARE APPROXIMATE. CONFIRM THE LOCATION OF THE MAINTENANCE HOLES AND DUCTBANKS WITH THE CONTRACTING OFFICER. OBTAIN CONTRACTING OFFICER APPROVAL OF MAINTENANCE HOLE LOCATIONS AND ORIENTATION PRIOR TO THE COMMENCEMENT OF WORK.
- F. SEE SHEET TS701 TELECOMMUNICATIONS INTERBUILDING BACKBONE RISER FOR PROJECT CABLING REQUIREMENTS.

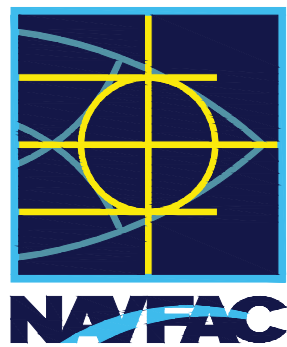

Jacobs **BURNS & MCDONNELL**
JACOBSRAM, A JOINT VENTURE
1100 NORTH GLEBE ROAD
SUITE 500
ARLINGTON, VA 22201

APPROVED
FOR COMMANDER NAVFAC DATE 04/10/2026

ACTIVITY
AFMISC APPROVAL PER NAVFAC SAT-TO CHECKLIST

SATISFACTORY TO DATE 31 DEC 2025

DES: TGB DRW: BDP REV: SDS

PMIDM KKK

BRANCH MANAGER SMK

CHIEF ENGINEER SMK

FIRE PROTECTION RO

DEPARTMENT OF THE NAVY

NAVAL FACILITIES ENGINEERING SYSTEMS COMMAND

NAVAL FACILITIES ENGINEERING SYSTEMS COMMAND - PACIFIC

JOINT REGION MARIANAS (JRM)

GUAM

ANDERSEN AIR FORCE BASE

FY24 AUJY183012 (P-012)

PDI: NORTH AIRCRAFT PARKING RAMP

TELECOMMUNICATIONS SITE PLAN 4

SCALE: AS SHOWN

EPROJETS NO.: 1665555

CONSTR CONTROL NO.

NAVFAC DRAWING NO.

17361920

SHEET 207 OF 377

TS104

A

B

C

D

REDESIGN FINAL SUBMITTAL

FILE NAME: \\bmcdburnsmcd.com\dis\clients\USNavy\pac\133097_Guam\PO12\NAE\Design\Telecom\TS105.dwg
LAYOUT NAME: TS105
PLOT DATE: 03/10/2026 3:53pm
USER: bdpinkley

D


C

B

A

MATCHLINE SEE TS102

MATCHLINE SEE TS104

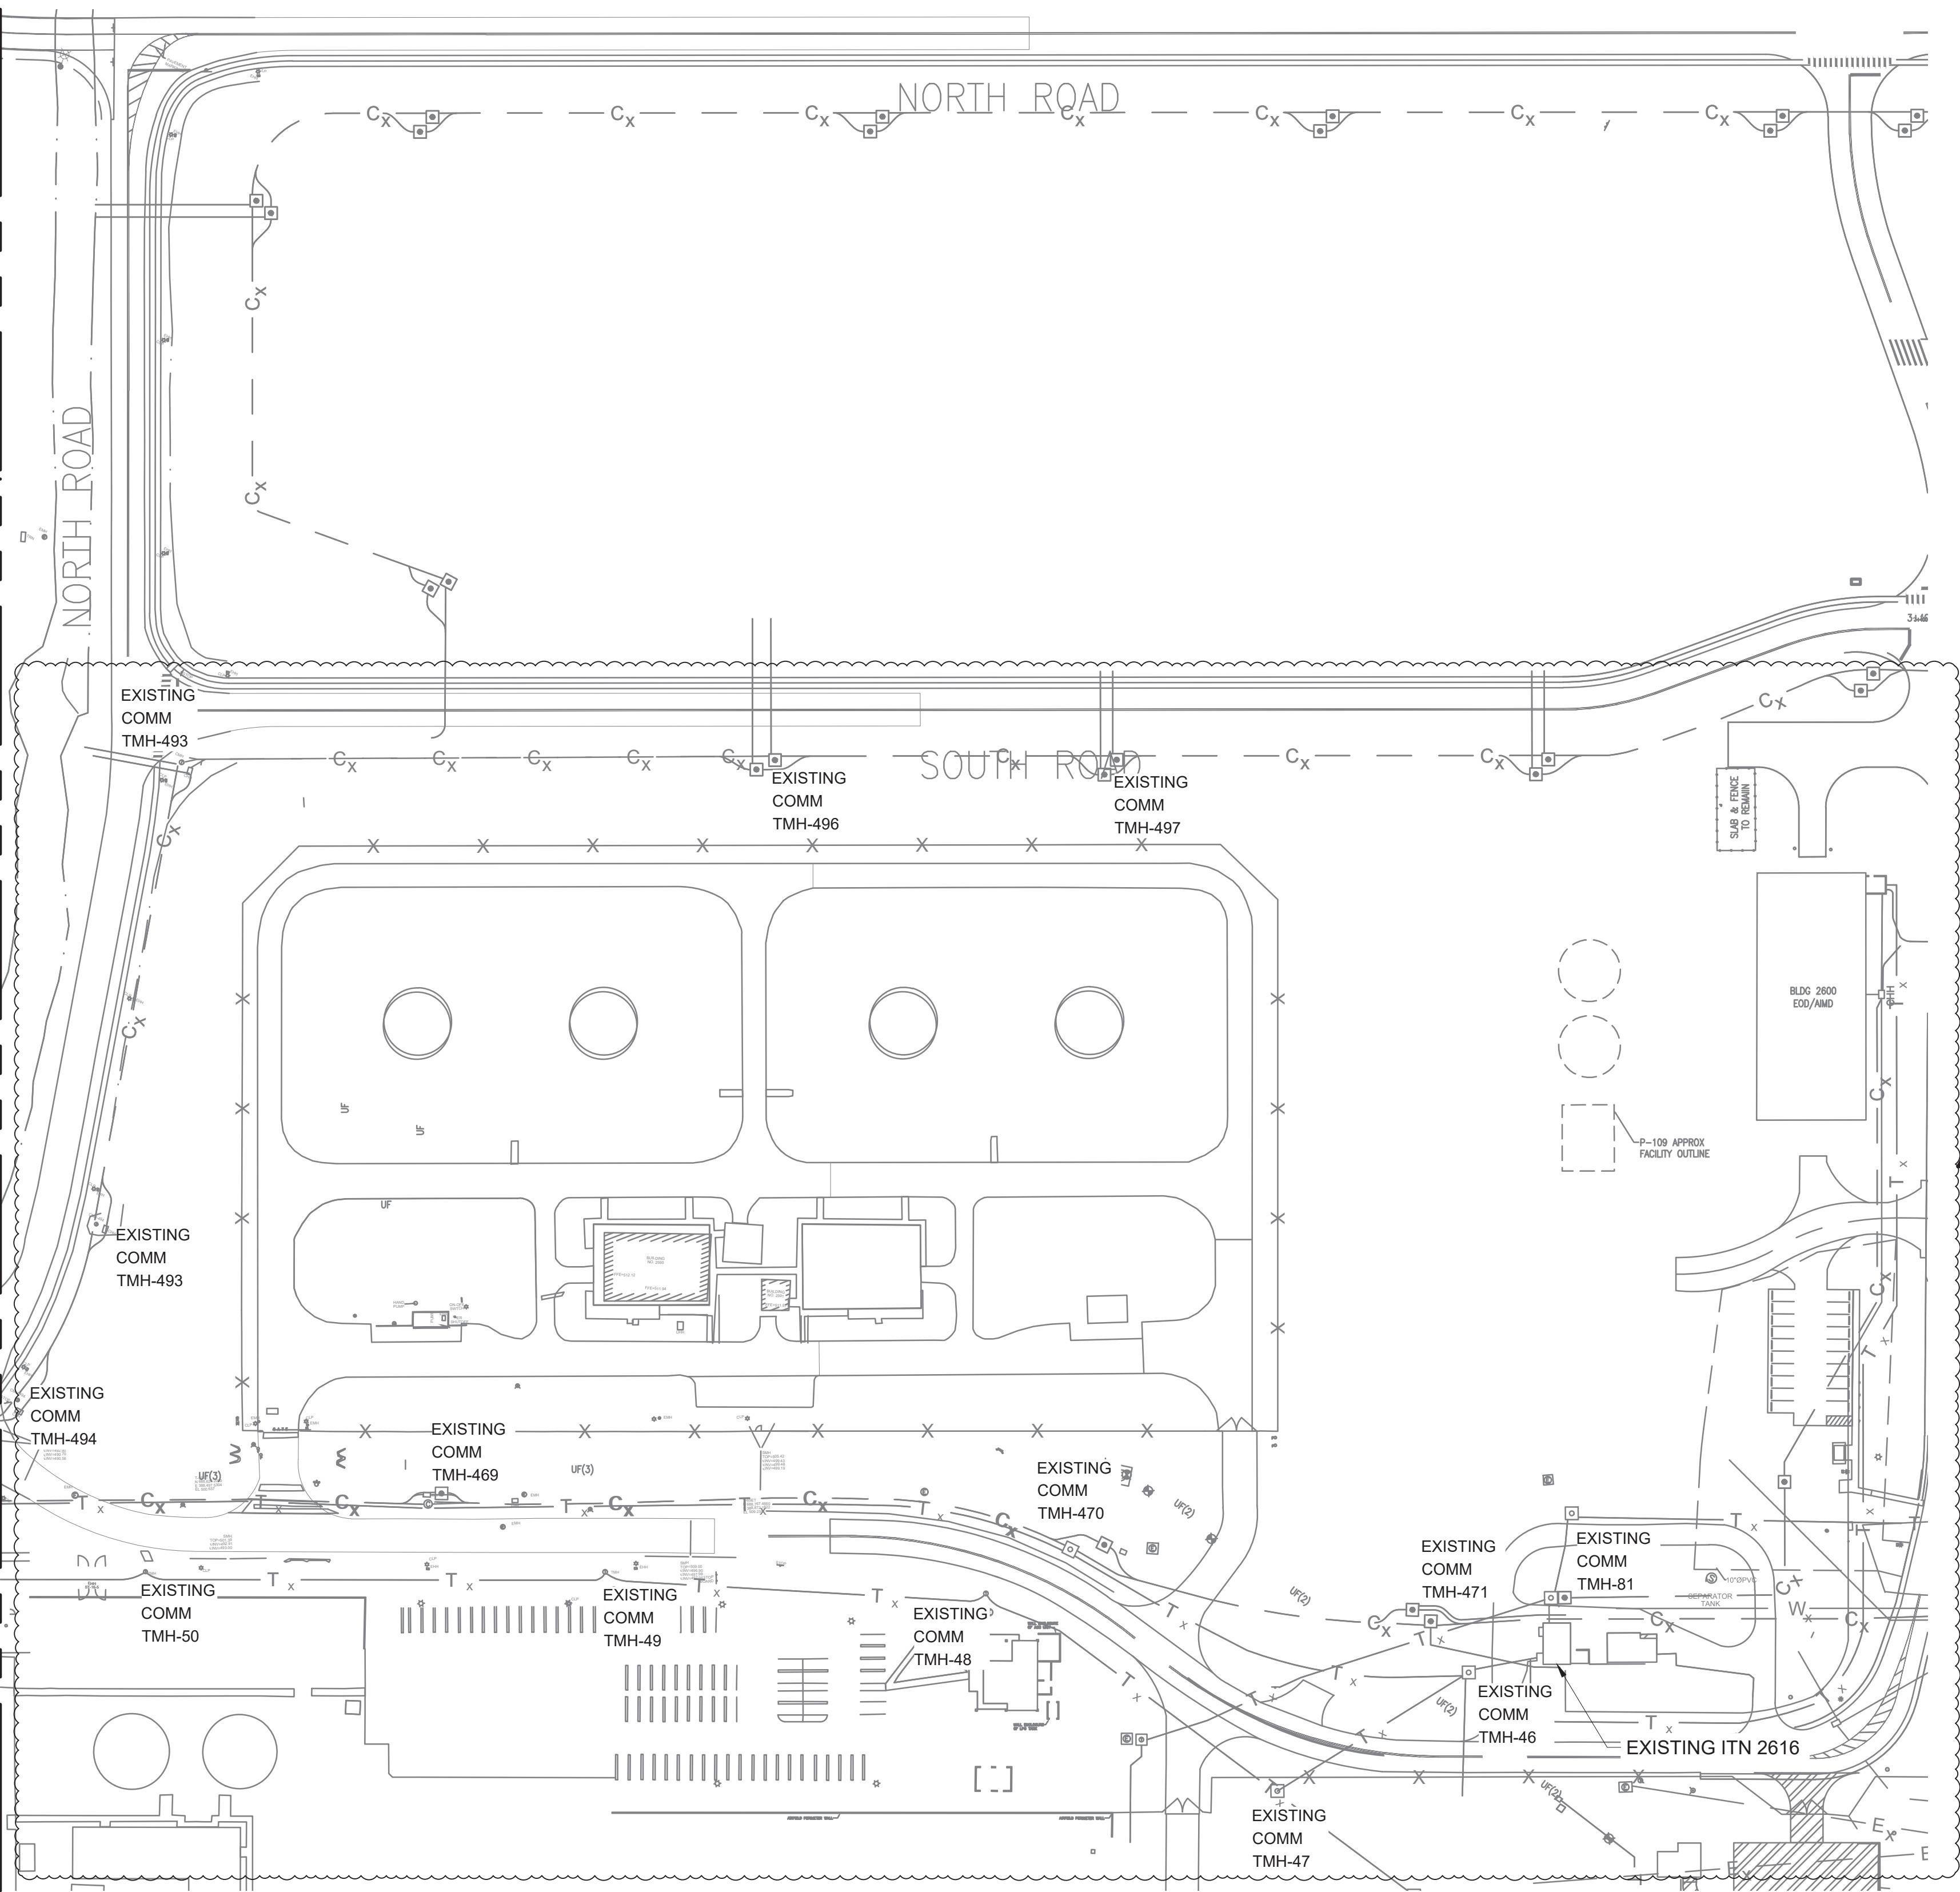

A1

TELECOMMUNICATIONS SITE PLAN 5

SCALE 1"=80'




GRAPHIC SCALE




SCALE: 1"=80'

NORTH ARROW

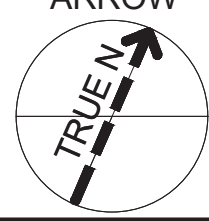

GENERAL NOTES - SITE PLANS

- A. THESE DRAWINGS ARE SUPPLEMENTAL TO THE PROJECT SPECIFICATIONS, ARE SCHEMATIC IN NATURE AND MUST NOT BE USED FOR FIELD INSTALLATION. FIELD INSTALLATION MUST BE IN ACCORDANCE WITH APPROVED SHOP DRAWINGS. SEE PROJECT SPECIFICATIONS FOR SHOP DRAWING REQUIREMENTS. THE LAYOUT OF TELECOMMUNICATIONS EQUIPMENT MUST BE FULLY COORDINATED WITH OTHER TRADES AND EQUIPMENT PRIOR TO SUBMISSION OF SHOP DRAWINGS FOR APPROVAL.
- B. SEE SHEET TS001 FOR PROJECT GENERAL NOTES, SYMBOL LEGEND AND ABBREVIATIONS.
- C. COORDINATE MAINTENANCE HOLE PLACEMENT SCHEDULE WITH CONTRACTING OFFICER SUCH THAT PLACEMENT CAN BE WITNESSED BY GOVERNMENT.
- D. COORDINATE DUCTBANK INSPECTION WITH CONTRACTING OFFICER SUCH THAT GOVERNMENT MAY INSPECT PRIOR TO POURING CONCRETE REINFORCEMENT.
- E. LOCATIONS OF MAINTENANCE HOLES AND DUCTBANKS ARE APPROXIMATE. CONFIRM THE LOCATION OF THE MAINTENANCE HOLES AND DUCTBANKS WITH THE CONTRACTING OFFICER. OBTAIN CONTRACTING OFFICER APPROVAL OF MAINTENANCE HOLE LOCATIONS AND ORIENTATION PRIOR TO THE COMMENCEMENT OF WORK.
- F. SEE SHEET TS701 TELECOMMUNICATIONS INTERBUILDING BACKBONE RISER FOR PROJECT CABLING REQUIREMENTS.

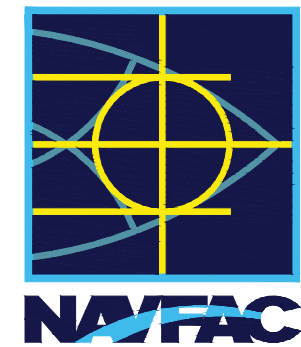

Jacobs **BURNS & MCDONNELL**
JACOBSRAM, A JOINT VENTURE
1100 NORTH GLEBE ROAD
SUITE 500
ARLINGTON, VA 22201

APPROVED
DATE: 04/10/2026
FOR COMMANDER NAVFAC

ACTIVITY
AFINISC APPROVAL PER NAVFAC
SAT-TO CHECKLIST

SATISFACTORY TO DATE 31 DEC 2025

DES: TOR DRW: BDP REV: SDS

PM/DM KKK

BRANCH MANAGER SMK

CHIEF ENGINEER SMK

FIRE PROTECTION RO

GUAM

NAVFAC PACIFIC

ANDERSEN AIR FORCE BASE

NAVAL FACILITIES ENGINEERING SYSTEMS COMMAND

NAVAL FACILITIES ENGINEERING SYSTEMS COMMAND - PACIFIC

JOINT REGION MARIANAS (JRM)

PDI: NORTH AIRCRAFT PARKING RAMP

TELECOMMUNICATIONS SITE PLAN 5

FY24 AUJY183012 (P-012)

AS SHOWN

EPROJECTS NO.: 1665555

CONSTR CONTROL NO.

NAVFAC DRAWING NO.

17361921

SHEET 208 OF 377

TS105

REDESIGN FINAL SUBMITTAL

FILE NAME: \\bmcdburnsmcd.com\dis\clients\NAV\USNavy\Loc\Guam\012NAR\Design\Elec\Sheets\1665555_TS101-TS105.dwg
LAYOUT NAME: TS106
PLOTTED: 03/10/2026 3:54pm
USER: bdpinkley

D

C

B

A


A1

TELECOMMUNICATIONS SITE PLAN 6

SCALE 1" = 80'

MATCHLINE, SEE TS107

MATCHLINE, SEE TS101

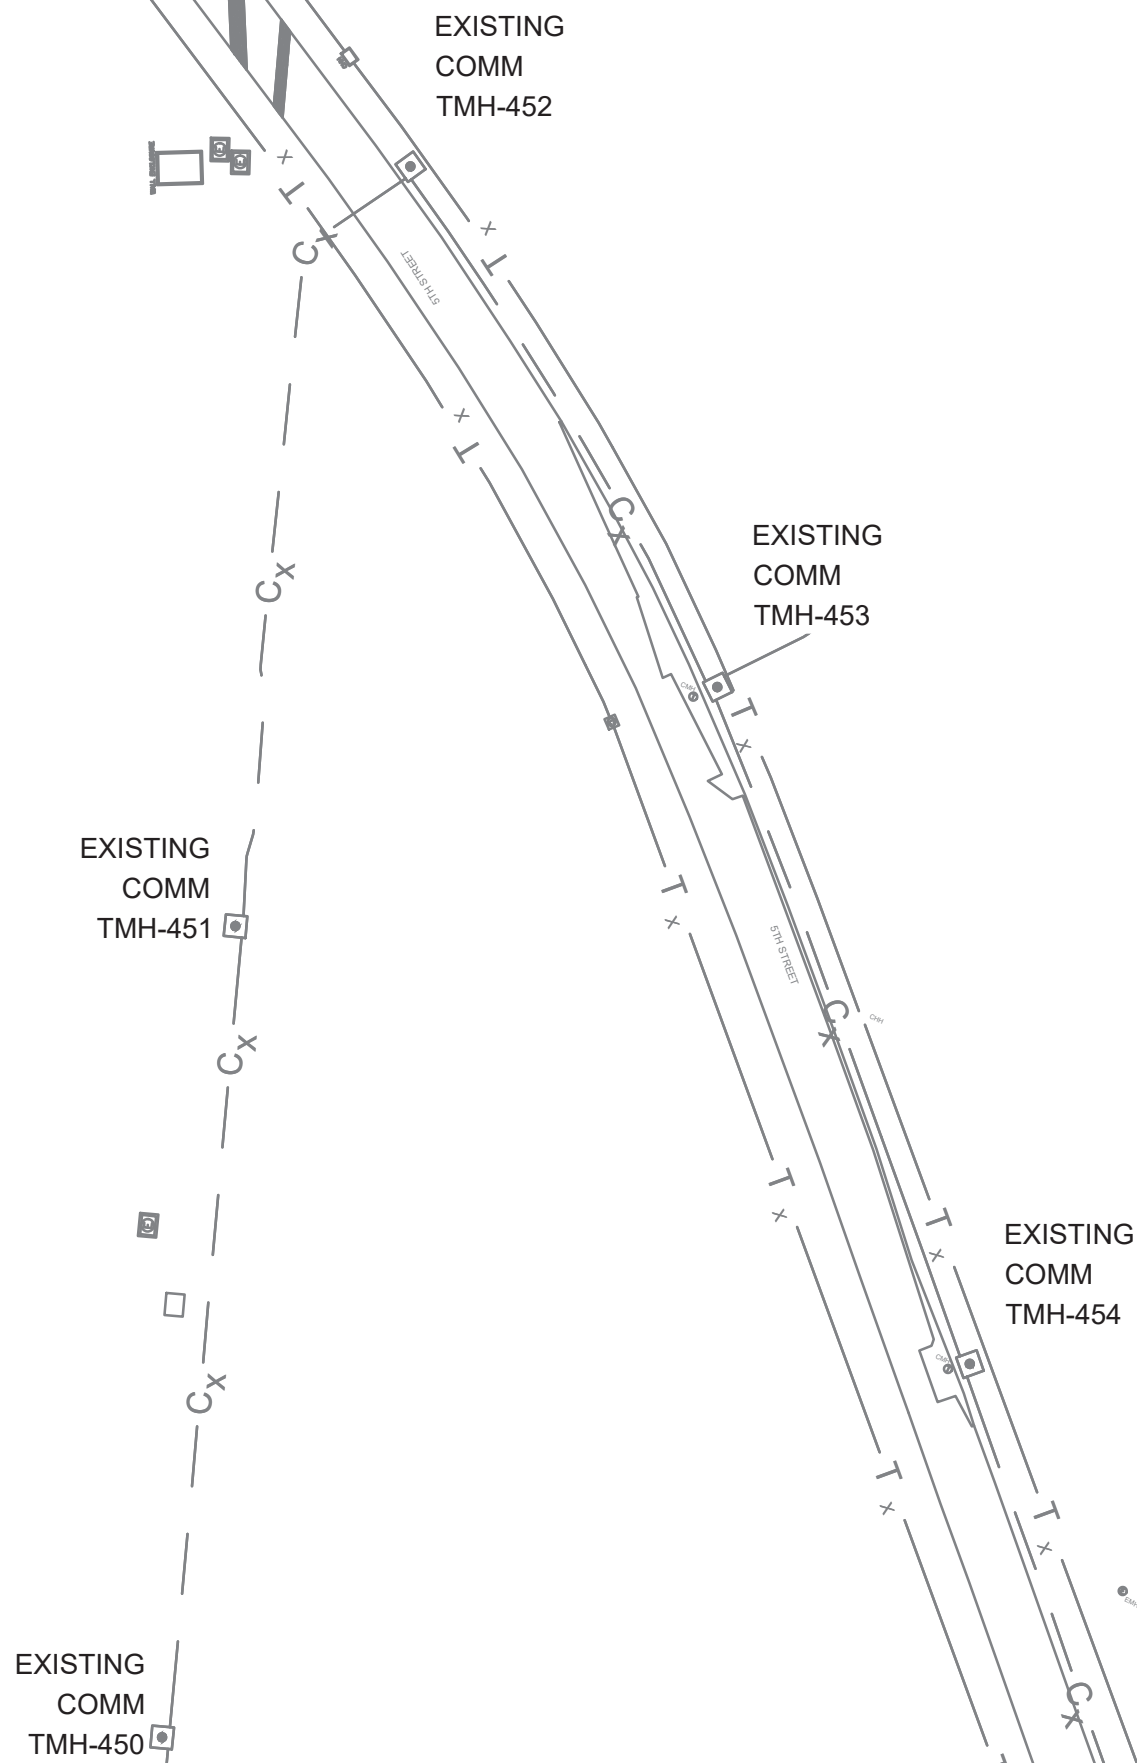

GENERAL NOTES - SITE PLANS

- A. THESE DRAWINGS ARE SUPPLEMENTAL TO THE PROJECT SPECIFICATIONS, ARE SCHEMATIC IN NATURE AND MUST NOT BE USED FOR FIELD INSTALLATION. FIELD INSTALLATION MUST BE IN ACCORDANCE WITH APPROVED SHOP DRAWINGS. SEE PROJECT SPECIFICATIONS FOR SHOP DRAWING REQUIREMENTS. THE LAYOUT OF TELECOMMUNICATIONS EQUIPMENT MUST BE FULLY COORDINATED WITH OTHER TRADES AND EQUIPMENT PRIOR TO SUBMISSION OF SHOP DRAWINGS FOR APPROVAL.
- B. SEE SHEET TS001 FOR PROJECT GENERAL NOTES, SYMBOL LEGEND AND ABBREVIATIONS.
- C. COORDINATE MAINTENANCE HOLE PLACEMENT SCHEDULE WITH CONTRACTING OFFICER SUCH THAT PLACEMENT CAN BE WITNESSED BY GOVERNMENT.
- D. COORDINATE DUCTBANK INSPECTION WITH CONTRACTING OFFICER SUCH THAT GOVERNMENT MAY INSPECT PRIOR TO POURING CONCRETE REINFORCEMENT.
- E. LOCATIONS OF MAINTENANCE HOLES AND DUCTBANKS ARE APPROXIMATE. CONFIRM THE LOCATION OF THE MAINTENANCE HOLES AND DUCTBANKS WITH THE CONTRACTING OFFICER. OBTAIN CONTRACTING OFFICER APPROVAL OF MAINTENANCE HOLE LOCATIONS AND ORIENTATION PRIOR TO THE COMMENCEMENT OF WORK.
- F. SEE SHEET TS701 TELECOMMUNICATIONS INTERBUILDING BACKBONE RISER FOR PROJECT CABLING REQUIREMENTS.



JACOBS **BURNS & MCDONNELL**
JACOBSRAM, A JOINT VENTURE
1100 NORTH GLEBE ROAD
SUITE 500
ARLINGTON, VA 22201

APPROVED
Date: 04/10/2026
FOR COMMANDER NAVFAC DATE 04/10/2026

ACTIVITY
AFMISC APPROVAL PER NAVFAC
SAT-TO CHECKLIST

SATISFACTORY TO DATE 31 DEC 2025

DES: TOR DRW: BDP REV: SDS


PMIDM KKK

BRANCH MANAGER SMK

CHIEF ENGINEER SMK

FIRE PROTECTION RO

DEPARTMENT OF THE NAVY
NAVAL FACILITIES ENGINEERING SYSTEMS COMMAND
NAVAL FACILITIES ENGINEERING SYSTEMS COMMAND - PACIFIC
JOINT REGION MARIANAS (JRM)
ANDERSEN AIR FORCE BASE
GUAM
FY24 AUJY183012 (P-012)
PDI: NORTH AIRCRAFT PARKING RAMP
TELECOMMUNICATIONS SITE PLAN 6

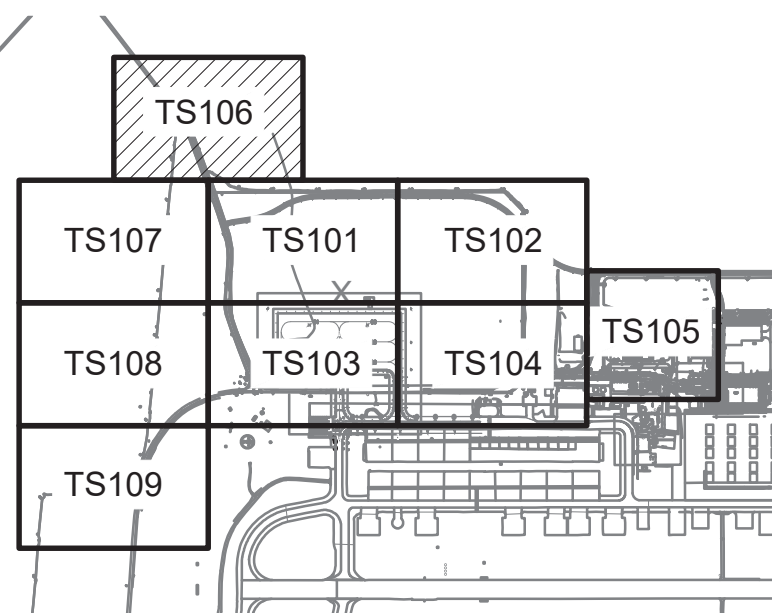

AREA KEY MAP




GRAPHIC SCALE

0 40' 80' 160'

SCALE: 1"=80'

NORTH
ARROW

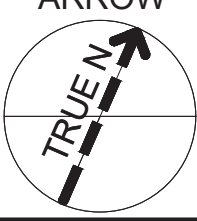

SCALE: AS SHOWN
EPROJECTS NO.: 1665555
CONSTR CONTROL NO.
NAVFAC DRAWING NO. 17362001
SHEET 298 OF 377
TS106

IF SHEET IS LESS THAN 22" X 34"
REDUCED PRINT. USE GRAPHIC SCALES

A

B

C

D

REDESIGN FINAL SUBMITTAL

FILE NAME: \\bmcdburnsmcd.com\dis\clients\Navy\USNavy\pac\133097_Guam\PO12NAR_Design\Elec\Sheets\PO12_1665555_TS101-TS105.dwg
LAYOUT NAME: TS107
PLOTTED: 03/10/2026 3:54pm
USER: bdpinkley

D

C

B

A

A1

TELECOMMUNICATIONS SITE PLAN 7

SCALE 1" = 80'

MATCHLINE, SEE TS108

EXISTING
COMM
TMH-447

EXISTING
COMM
TMH-448


EXISTING
COMM
TMH-449

MATCHLINE, SEE TS106

GENERAL NOTES - SITE PLANS

- A. THESE DRAWINGS ARE SUPPLEMENTAL TO THE PROJECT SPECIFICATIONS, ARE SCHEMATIC IN NATURE AND MUST NOT BE USED FOR FIELD INSTALLATION. FIELD INSTALLATION MUST BE IN ACCORDANCE WITH APPROVED SHOP DRAWINGS. SEE PROJECT SPECIFICATIONS FOR SHOP DRAWING REQUIREMENTS. THE LAYOUT OF TELECOMMUNICATIONS EQUIPMENT MUST BE FULLY COORDINATED WITH OTHER TRADES AND EQUIPMENT PRIOR TO SUBMISSION OF SHOP DRAWINGS FOR APPROVAL.
- B. SEE SHEET TS001 FOR PROJECT GENERAL NOTES, SYMBOL LEGEND AND ABBREVIATIONS.
- C. COORDINATE MAINTENANCE HOLE PLACEMENT SCHEDULE WITH CONTRACTING OFFICER SUCH THAT PLACEMENT CAN BE WITNESSED BY GOVERNMENT.
- D. COORDINATE DUCTBANK INSPECTION WITH CONTRACTING OFFICER SUCH THAT GOVERNMENT MAY INSPECT PRIOR TO POURING CONCRETE REINFORCEMENT.
- E. LOCATIONS OF MAINTENANCE HOLES AND DUCTBANKS ARE APPROXIMATE. CONFIRM THE LOCATION OF THE MAINTENANCE HOLES AND DUCTBANKS WITH THE CONTRACTING OFFICER. OBTAIN CONTRACTING OFFICER APPROVAL OF MAINTENANCE HOLE LOCATIONS AND ORIENTATION PRIOR TO THE COMMENCEMENT OF WORK.
- F. SEE SHEET TS701 TELECOMMUNICATIONS INTERBUILDING BACKBONE RISER FOR PROJECT CABLING REQUIREMENTS.

MATCHLINE, SEE TS101

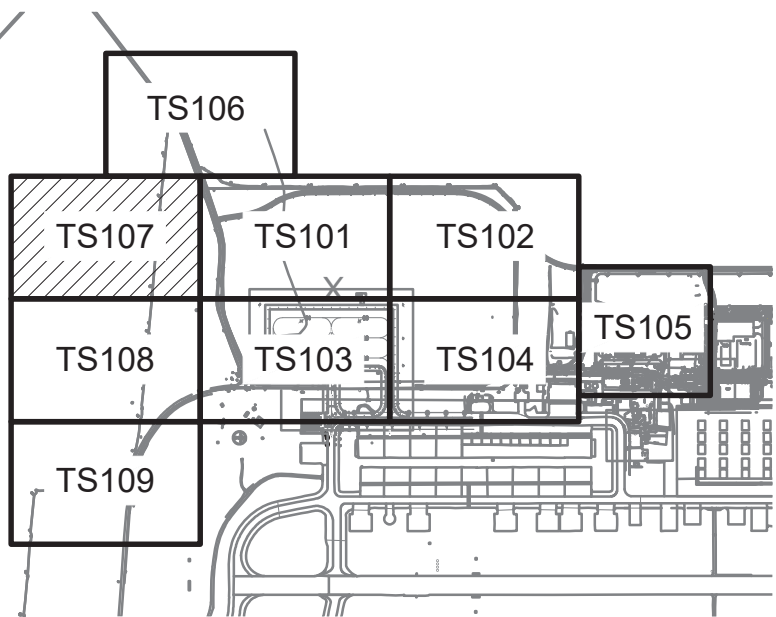

AREA KEY MAP




GRAPHIC SCALE


0 40' 80' 160'

SCALE: 1"=80'

NORTH
ARROW

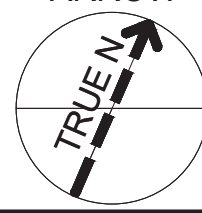

SCALE:	AS SHOWN
EPROJECTS NO.:	1665555
CONSTR CONTROL NO.	
NAVAFAC DRAWING NO.	17362002
SHEET	299.2 OF 377
A1 TS107	

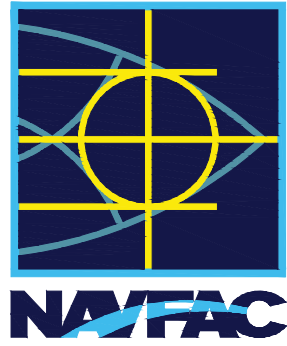

Jacobs **BURNS & MCDONNELL**
JACOBSBAM, A JOINT VENTURE
1100 NORTH GLEBE ROAD
SUITE 500
ARLINGTON, VA 22201

APPROVED
FOR COMMANDER NAVFAC DATE 04/10/2026

ACTIVITY
AFMISC APPROVAL PER NAVFAC
SAT-TO CHECKLIST

SATISFACTORY TO DATE 31 DEC 2025

DES: TOR DRW: BDP REV: SDS

PMIDM KKK

BRANCH MANAGER SMK

CHIEF ENGINEER SMK

FIRE PROTECTION RO

DEPARTMENT OF THE NAVY
NAVAL FACILITIES ENGINEERING SYSTEMS COMMAND
NAVFAC PACIFIC
ANDERSEN AIR FORCE BASE
GUAM

FY24 AUJY183012 (P-012).
PDI: NORTH AIRCRAFT PARKING RAMP
TELECOMMUNICATIONS SITE PLAN 7

A

REDESIGN FINAL SUBMITTAL

IF SHEET IS LESS THAN 22" X 34"
REDUCED PRINT. USE GRAPHIC SCALES

FILE NAME: \\bmcdburnsmcd.com\dis\clients\NAVFAC\USNavy\pac\133097_Guam\PO12NAR\Design\Sheets\PO12_1665555_TS101-TS105.dwg
LAYOUT NAME: TS108
PLOTTED: 03/10/2026 3:54pm
USER: bdpinkley

D

C

B

A

MATCHLINE, SEE TS107

MATCHLINE, SEE TS109

EXISTING
COMM
TMH-446

EXISTING
COMM
TMH-445

EXISTING
COMM
TMH-444

EXISTING
COMM
TMH-60


A1

TELECOMMUNICATIONS SITE PLAN 8

SCALE 1" = 80'

GENERAL NOTES - SITE PLANS

- A. THESE DRAWINGS ARE SUPPLEMENTAL TO THE PROJECT SPECIFICATIONS, ARE SCHEMATIC IN NATURE AND MUST NOT BE USED FOR FIELD INSTALLATION. FIELD INSTALLATION MUST BE IN ACCORDANCE WITH APPROVED SHOP DRAWINGS. SEE PROJECT SPECIFICATIONS FOR SHOP DRAWING REQUIREMENTS. THE LAYOUT OF TELECOMMUNICATIONS EQUIPMENT MUST BE FULLY COORDINATED WITH OTHER TRADES AND EQUIPMENT PRIOR TO SUBMISSION OF SHOP DRAWINGS FOR APPROVAL.
- B. SEE SHEET TS001 FOR PROJECT GENERAL NOTES, SYMBOL LEGEND AND ABBREVIATIONS.
- C. COORDINATE MAINTENANCE HOLE PLACEMENT SCHEDULE WITH CONTRACTING OFFICER SUCH THAT PLACEMENT CAN BE WITNESSED BY GOVERNMENT.
- D. COORDINATE DUCTBANK INSPECTION WITH CONTRACTING OFFICER SUCH THAT GOVERNMENT MAY INSPECT PRIOR TO POURING CONCRETE REINFORCEMENT.
- E. LOCATIONS OF MAINTENANCE HOLES AND DUCTBANKS ARE APPROXIMATE. CONFIRM THE LOCATION OF THE MAINTENANCE HOLES AND DUCTBANKS WITH THE CONTRACTING OFFICER. OBTAIN CONTRACTING OFFICER APPROVAL OF MAINTENANCE HOLE LOCATIONS AND ORIENTATION PRIOR TO THE COMMENCEMENT OF WORK.
- F. SEE SHEET TS701 TELECOMMUNICATIONS INTERBUILDING BACKBONE RISER FOR PROJECT CABLING REQUIREMENTS.

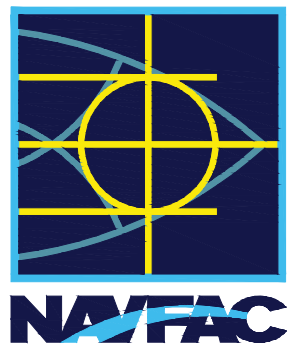

JACOBS **BURNS & MCDONNELL**
JACOBSBAM, A JOINT VENTURE
1100 NORTH GLEBE ROAD
SUITE 500
ARLINGTON, VA 22201

APPROVED
DATE: 04/10/2026
FOR COMMANDER NAVFAC

ACTIVITY
AFMISC APPROVAL PER NAVFAC
SAT-TO CHECKLIST

SATISFACTORY TO DATE 31 DEC 2026

DES: TGB DRW: BDP REV: SDS

PMIDM KKK

BRANCH MANAGER SMK

CHIEF ENGINEER SMK

FIRE PROTECTION RO

DEPARTMENT OF THE NAVY
NAVAL FACILITIES ENGINEERING SYSTEMS COMMAND
NAVFAC PACIFIC
ANDERSEN AIR FORCE BASE
GUAM

FY24 AUJY183012 (P-012)
PDI: NORTH AIRCRAFT PARKING RAMP
TELECOMMUNICATIONS SITE PLAN 8


SCALE: AS SHOWN
EPROJECTS NO.: 1665555
CONSTR CONTROL NO.
NAVFAC DRAWING NO. 17362003
SHEET 299.3 OF 377
TS108

GRAPHIC SCALE

0 40' 80' 160'

SCALE: 1"=80'

NORTH
ARROW

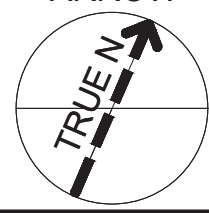

IF SHEET IS LESS THAN 22" X 34"
REDUCED PRINT. USE GRAPHIC SCALES

REDESIGN FINAL SUBMITTAL

FILE NAME: \\bmcdburnsmcd.com\dis\clients\USNavy\pac\133097_Guam\012NAR_Design\Elec\Sheets\012_1665555_TS101-TS105.dwg
LAYOUT NAME: TS109
PLOTTED: 03/10/2026 3:55pm
USER: bdpinkley

D

C


B

A

A1


TELECOMMUNICATIONS SITE PLAN 9

SCALE 1" = 80'

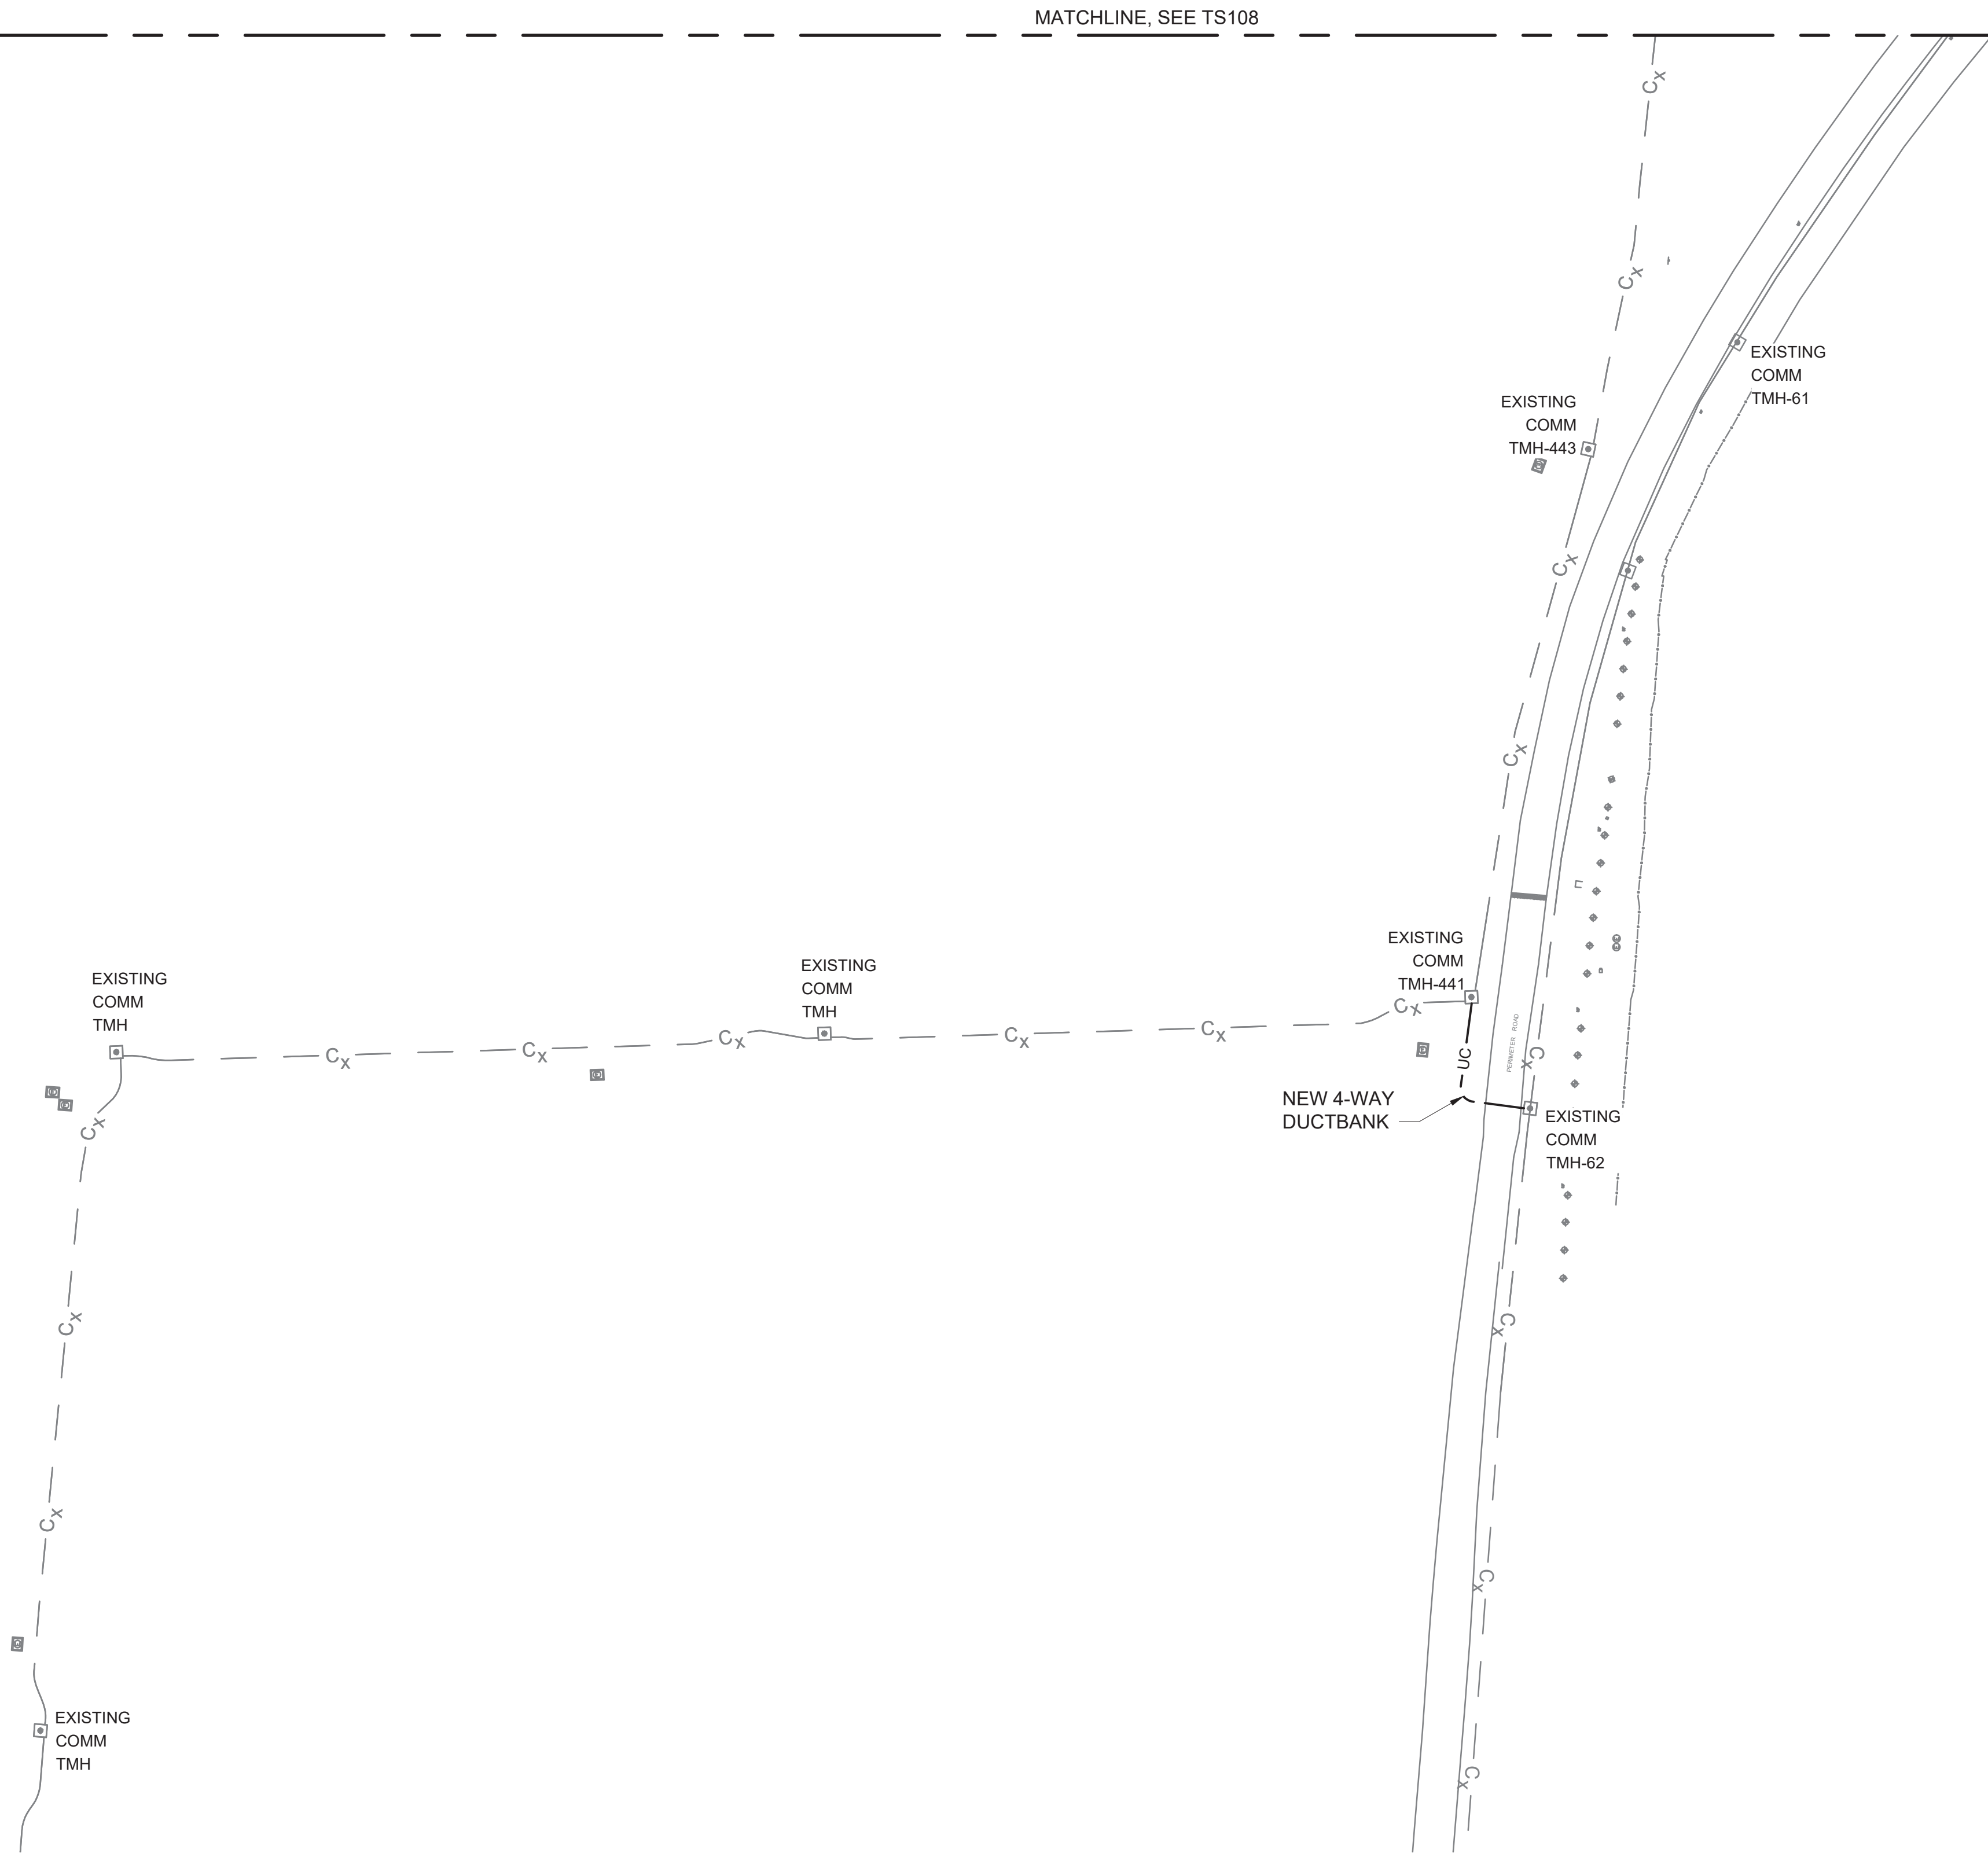

GENERAL NOTES - SITE PLANS

- A. THESE DRAWINGS ARE SUPPLEMENTAL TO THE PROJECT SPECIFICATIONS, ARE SCHEMATIC IN NATURE AND MUST NOT BE USED FOR FIELD INSTALLATION. FIELD INSTALLATION MUST BE IN ACCORDANCE WITH APPROVED SHOP DRAWINGS. SEE PROJECT SPECIFICATIONS FOR SHOP DRAWING REQUIREMENTS. THE LAYOUT OF TELECOMMUNICATIONS EQUIPMENT MUST BE FULLY COORDINATED WITH OTHER TRADES AND EQUIPMENT PRIOR TO SUBMISSION OF SHOP DRAWINGS FOR APPROVAL.
- B. SEE SHEET TS001 FOR PROJECT GENERAL NOTES, SYMBOL LEGEND AND ABBREVIATIONS.
- C. COORDINATE MAINTENANCE HOLE PLACEMENT SCHEDULE WITH CONTRACTING OFFICER SUCH THAT PLACEMENT CAN BE WITNESSED BY GOVERNMENT.
- D. COORDINATE DUCTBANK INSPECTION WITH CONTRACTING OFFICER SUCH THAT GOVERNMENT MAY INSPECT PRIOR TO POURING CONCRETE REINFORCEMENT.
- E. LOCATIONS OF MAINTENANCE HOLES AND DUCTBANKS ARE APPROXIMATE. CONFIRM THE LOCATION OF THE MAINTENANCE HOLES AND DUCTBANKS WITH THE CONTRACTING OFFICER. OBTAIN CONTRACTING OFFICER APPROVAL OF MAINTENANCE HOLE LOCATIONS AND ORIENTATION PRIOR TO THE COMMENCEMENT OF WORK.
- F. SEE SHEET TS701 TELECOMMUNICATIONS INTERBUILDING BACKBONE RISER FOR PROJECT CABLING REQUIREMENTS.

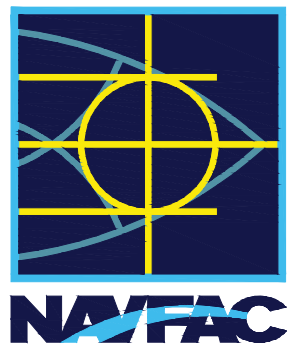

APPROVED
FOR COMMANDER NAVFAC DATE 04/10/2026

ACTIVITY
AFMISC APPROVAL PER NAVFAC SAT-TO CHECKLIST

SATISFACTORY TO DATE 31 DEC 2026

DES: TGB DRW: BDP REV: SDS

PM/DM KKK

BRANCH MANAGER SMK

CHIEF ENGINEER SMK

FIRE PROTECTION RO

GUAM

NAVAL FACILITIES ENGINEERING SYSTEMS COMMAND

NAVAL FACILITIES ENGINEERING SYSTEMS COMMAND - PACIFIC

JOINT REGION MARIANAS (JRM)

ANDERSEN AIR FORCE BASE

FY24 AJJY183012 (P-012)

PDI: NORTH AIRCRAFT PARKING RAMP

TELECOMMUNICATIONS SITE PLAN 9

SCALE: AS SHOWN

EPROJECTS NO: 1665555

CONSTR CONTROL NO.

NAVFAC DRAWING NO. 17362004

SHEET 299.4 OF 377

TS109

GRAPHIC SCALE

0 40' 80' 160'

SCALE: 1"=80'

NORTH ARROW



IF SHEET IS LESS THAN 22" X 34"
REDUCED PRINT. USE GRAPHIC SCALES


A

B

C

D


REDESIGN FINAL SUBMITTAL

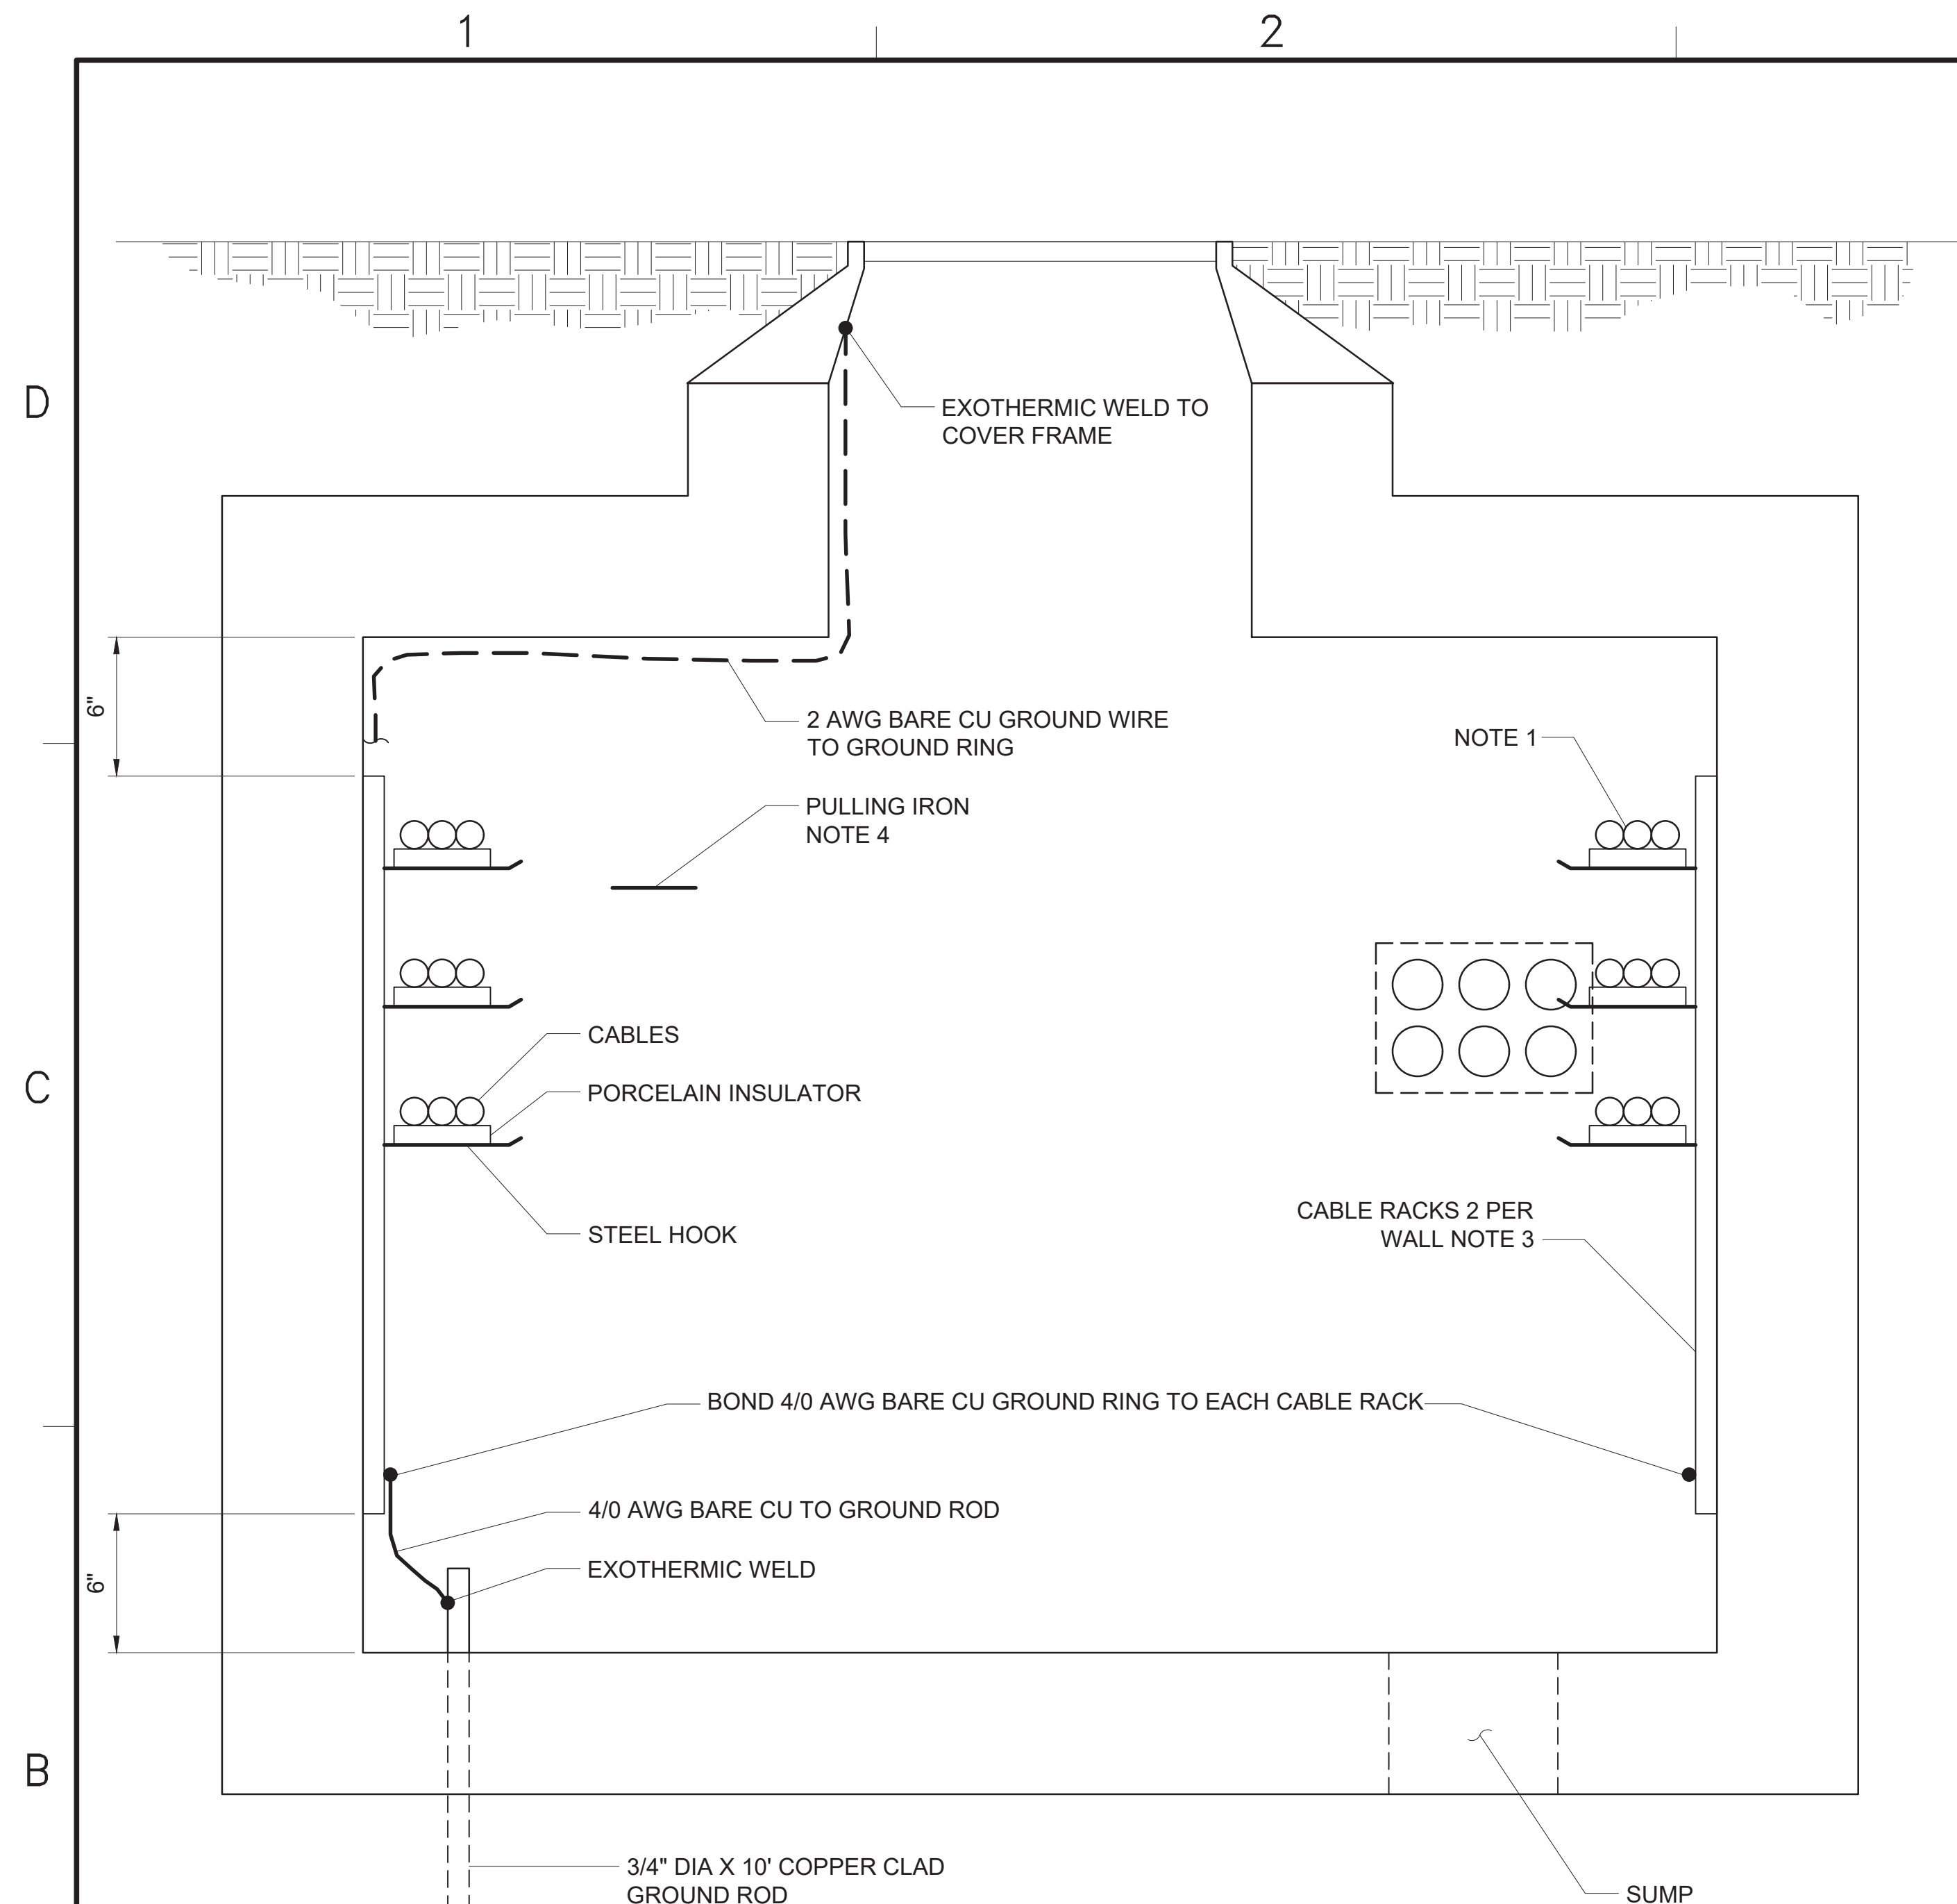


- NOTES:**

1. AT CABLE SPLICES ENCLOSURES, CONNECT SHIELDS TO GROUND RING W/ 6 AWG BARE CU.
2. LOCATE CABLE RACKS 30" FROM ADJACENT WALL, EXCEPT VARY TO AVOID DUCT BANK ENTRANCE.
3. METALLIC EQUIPMENT MUST BE BONDED TO GROUND SO THEY ARE AT THE SAME POTENTIAL.

A1 COMMUNICATIONS MANHOLE EQUIPMENT DETAIL
SCALE: NTS

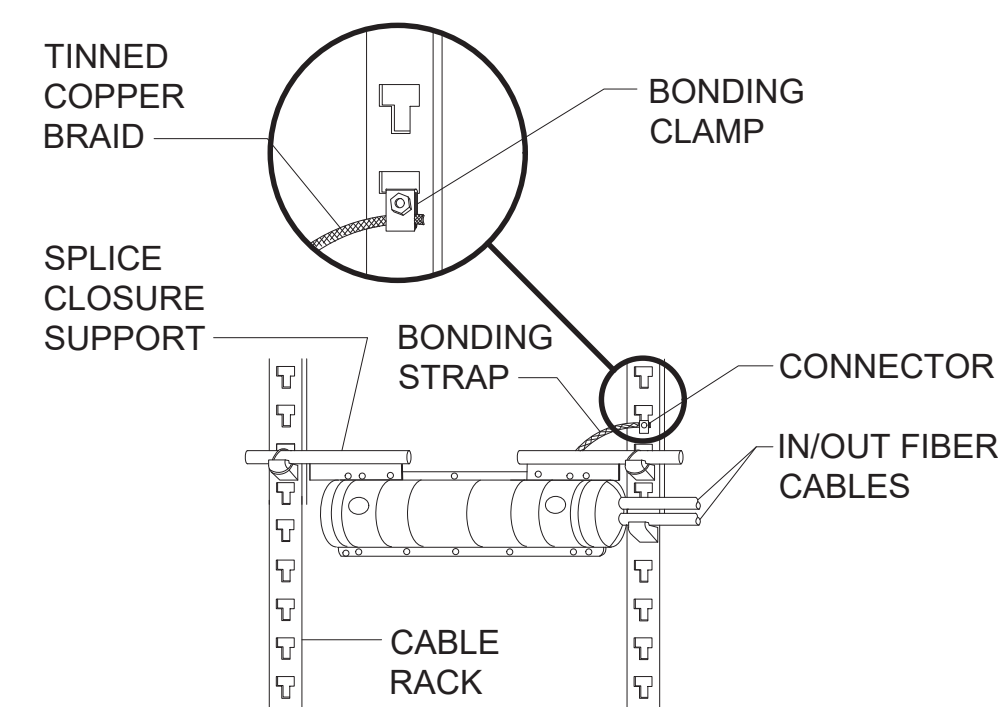


A3 MANHOLE/HAND HOLE RACKING DETAIL
SCALE: NTS

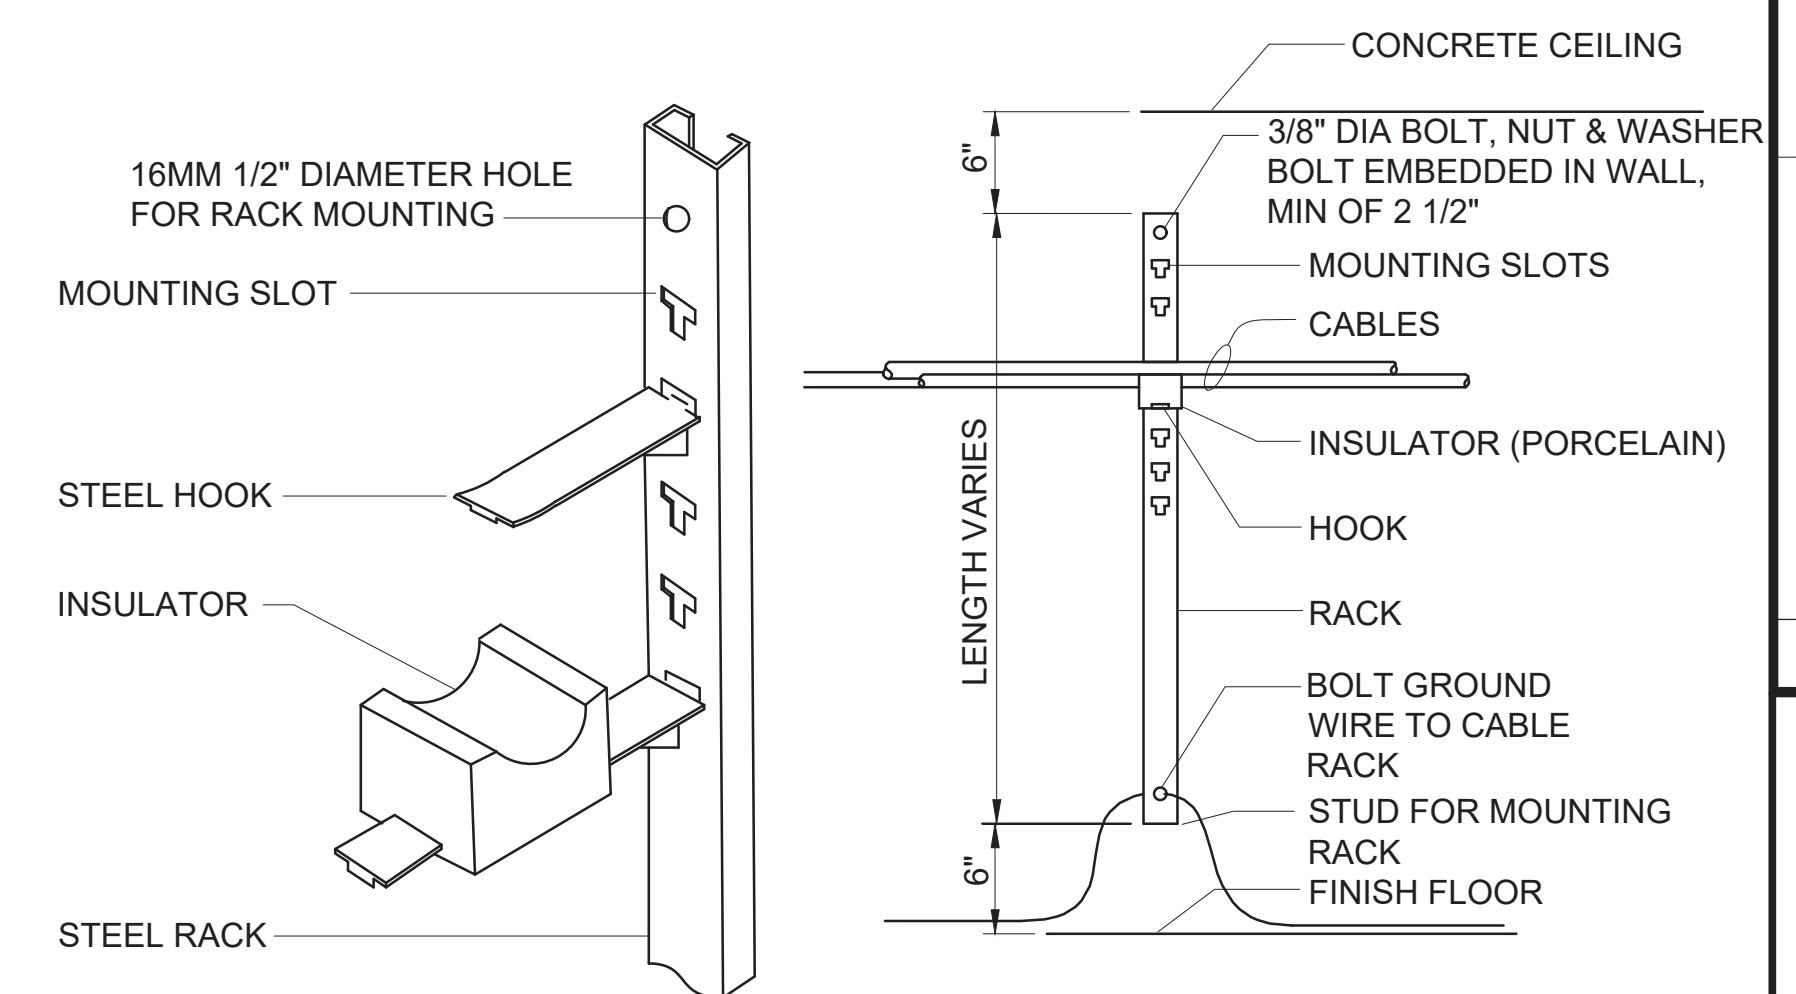

- NOTES:**

1. STEEL PARTS MUST BE HOT DIPPED GALVANIZED AFTER FABRICATION.
2. PROVIDE MINIMUM OF 2 CABLE RACKS PER RACKING WALL OF EACH MANHOLE. PROVIDE ADDITIONAL RACKS IN EXISTING MANHOLES & HANDHOLES TO RERACK CABLES AS REQUIRED.

C4 **CABLE RACK**
SCALE: NTS

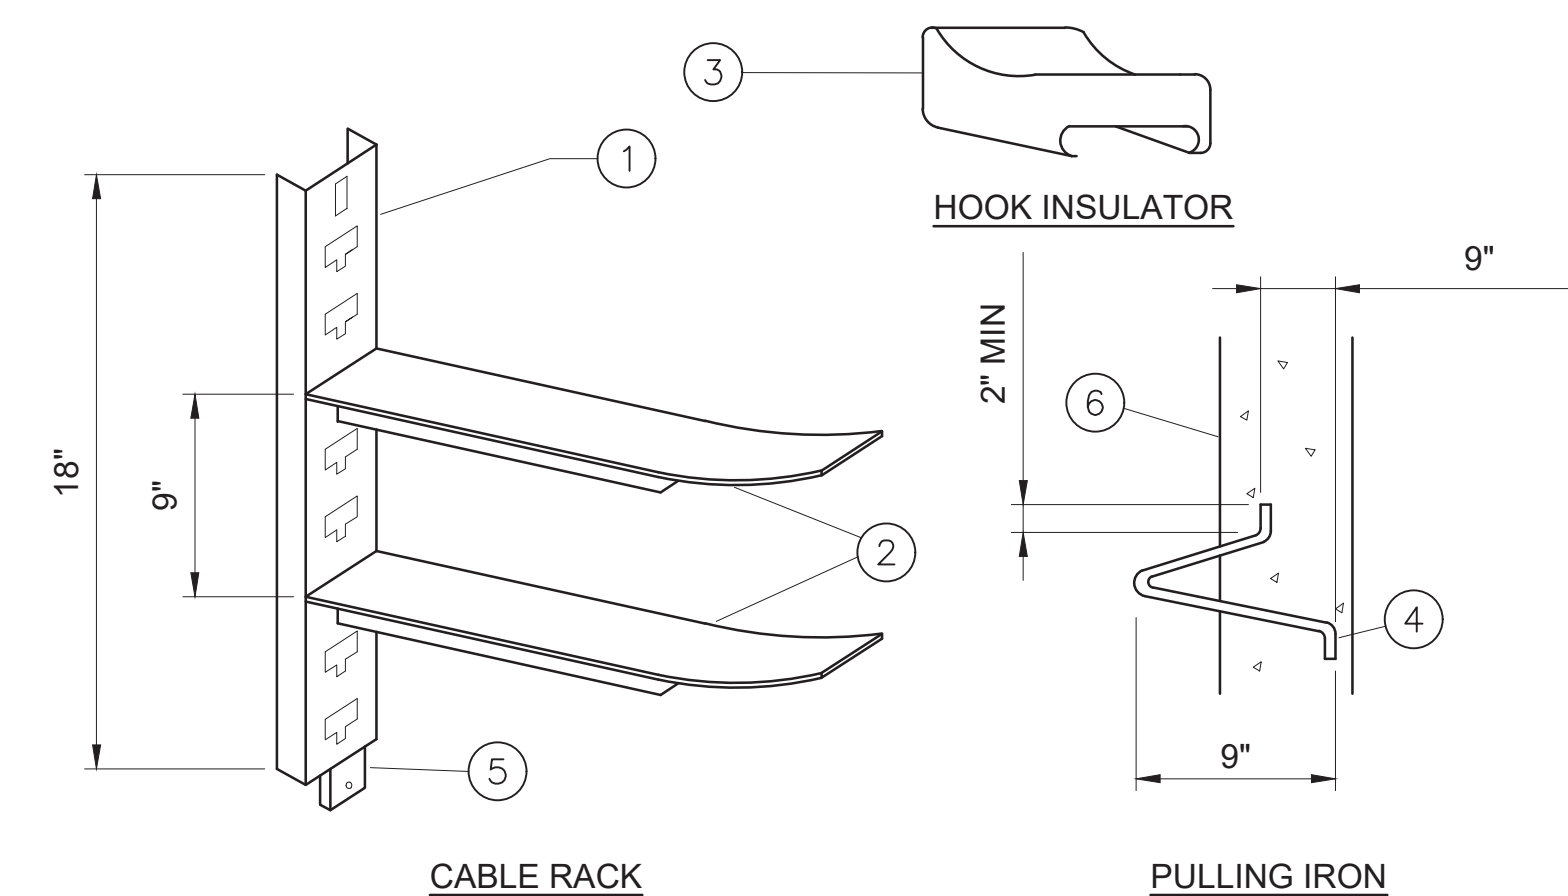

ITEM	BILL OF MATERIALS
1	CABLE RACK HOT DIP GALVANIZED
2	INSULATOR WELDED SUPPORT
3	HOOK INSULATOR 
4	PULLING IRON 1" DIA GALVANIZED
5	SLOT FOR 1/2" BOLT AND LEAD ANCHOR
6	THICK CONCRETE WALL AT 3000 PSI

- NOTES:**

1. PULLING IRON LOCATION IS ALWAYS OPPOSITE TO CONDUIT ENTRANCE.
2. PENETRATION POINT DESIGNATIONS ARE BASED ON THE MANHOLE LOCATION AS SHOWN ON THE CONSTRUCTION DRAWINGS. SUBMIT SHOP DRAWINGS FOR EACH MANHOLE FOR APPROVAL PRIOR TO FABRICATION.

CABLE RACK, INSULATOR, PULLING IRON DETAILS

SCALE: NTS



IF SHEET IS LESS THAN 22" X 34"
REDUCED PRINT. USE GRAPHIC SCALES

[illegible]

FILE NAME: C:\Revit\Projects\130097_E_Central_bdpinkley@burnsmcd.com.rvt
LAYOUT NAME: TELECOMMUNICATIONS INTERBUILDING BACKBONE RISER
PLOTED: 3/10/2026 3:50:44 PM
USER: BDP

D

C

B

A

COMMUNICATIONS BACKBONE CABLE SCHEDULE					
CABLE		TYPE	FROM ROOM	TO ROOM	DESCRIPTION
ID	QUANTITY				
X1	2-12 STRAND 3-72 STRAND 1-288 STRAND 2-144 STRAND	OS1 OSP SINGLE-MODE FIBER	EXISTING TMH-441	EXISTING TMH-467	THIS WORK MUST BE PERFORMED BEFORE EXISTING COMMUNICATION INFRASTRUCTURE CAN BE DEMOLISHED. COORDINATE CUTOVER WITH COMMUNICATION SQUADRON. PROVIDE (1) 3" 3-CELL FABRIC MESH INNERDUCT IN EXISTING PATHWAYS WHERE NEW CABLING WILL BE INSTALLED
X2	300 PAIR	PE-89 OSP COPPER	EXISTING TMH-441	EXISTING TMH-467	THIS WORK MUST BE PERFORMED BEFORE EXISTING COMMUNICATION INFRASTRUCTURE CAN BE DEMOLISHED. COORDINATE CUTOVER WITH COMMUNICATION SQUADRON. PROVIDE (1) 3" 3-CELL FABRIC MESH INNERDUCT IN EXISTING PATHWAYS WHERE NEW CABLING WILL BE INSTALLED
Z1	2-12 STRAND 3-72 STRAND 1-288 STRAND 2-144 STRAND	OS1 OSP SINGLE-MODE FIBER	ITN 2616	EXISTING BUILDINGS	COORDINATE CUTOVER WITH COMMUNICATION SQUADRON.
Z2	300 PAIR	PE-89 OSP COPPER	ITN 2616	EXISTING BUILDINGS	COORDINATE CUTOVER WITH COMMUNICATION SQUADRON.

GENERAL NOTES:

- A. THESE DRAWINGS ARE SUPPLEMENTAL TO THE PROJECT SPECIFICATIONS, ARE SCHEMATIC IN NATURE AND MUST NOT BE USED FOR FIELD INSTALLATION. FIELD INSTALLATION MUST BE IN ACCORDANCE WITH APPROVED SHOP DRAWINGS. SEE PROJECT SPECIFICATIONS FOR SHOP DRAWING REQUIREMENTS. THE LAYOUT OF TELECOMMUNICATIONS EQUIPMENT MUST BE FULLY COORDINATED WITH OTHER TRADES, EQUIPMENT AND FURNITURE WITHIN THE ROOM AND SPACE PRIOR TO SUBMISSION OF SHOP DRAWINGS FOR APPROVAL.
- B. SEE SHEET TS001 FOR PROJECT GENERAL NOTES, SYMBOL LEGEND AND ABBREVIATIONS.
- C. SEE TN100 SERIES SHEETS FOR TELECOMMUNICATION DUCTBANK ROUTING.

KEYED NOTES:

001. FIBER OPTIC SPLICE ENCLOSURE. COORDINATE SPLICE CUTOVER WITH BASE COMM SQUADRON.
002. COPPER SPLICE ENCLOSURE. COORDINATE SPLICE CUTOVER WITH BASE COMM SQUADRON.
003. CUT CABLING IN TMH-53 AND PULL BACK TO TMH-52. SPLICE EXISTING CABLING INTO NEW SPLICE ENCLOSURE IN TMH-467.
004. CUT CABLING IN TMH-61 AND PULL BACK TO TMH-62. SPLICE EXISTING CABLING INTO NEW SPLICE ENCLOSURE IN TMH-441.



JACOBS/B&M, A JOINT VENTURE
1100 NORTH GLEBE ROAD
SUITE 500
ARLINGTON, VA 22201
A/E Contract No. N6742-20-D-0002
A/E Task Order No. N6742-20-D-0002

APPROVED
Date: 04/10/2026
FOR COMMANDER NAVFAC DATE 04/10/2026

ACTIVITY
AFMISC APPROVAL PER NAVFAC
SAT-TO CHECKLIST

SATISFACTORY TO DATE 31 DEC 2025

DES: TOB DRW: BDP REV: SDS

PM/DM KKK

BRANCH MANAGER SMK

CHIEF ENG/ARCH SMK

FIRE PROTECTION RO

NAVAL FACILITIES ENGINEERING SYSTEMS COMMAND

NAVAL FACILITIES ENGINEERING SYSTEMS COMMAND - PACIFIC

JOINT REGION MARIANAS (JRM)

GUAM

FY24 AJY183012 (P-012).

PD: NORTH AIRCRAFT PARKING RAMP

TELECOMMUNICATIONS INTERBUILDING BACKBONE RISER

REDESIGN FINAL SUBMITTAL

SCALE: AS SHOWN

EPROJETS NO.: 1665555

CONSTR CONTROL NO.

NAVFAC DRAWING NO.

17361924

SHEET 301 OF 377

TS701

TELECOMMUNICATIONS INTERBUILDING BACKBONE RISER
DIAGRAM

A1 SCALE: NTS



IF SHEET IS LESS THAN 22" X 34"
REDUCED PRINT. USE GRAPHIC SCALES