



# Q-58 DATA CONCENTRATOR SHED RESTORATION

NAVAL STATION - NORFOLK, VIRGINIA

01/30/2026

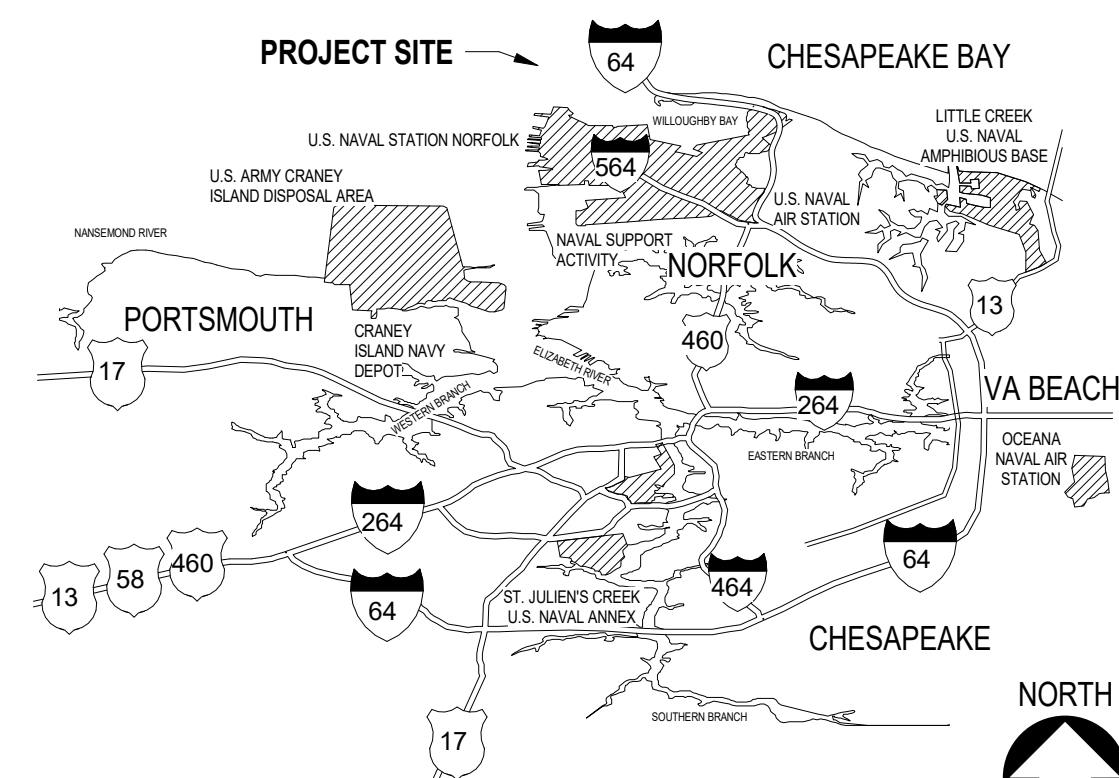

VICINITY MAP  
NOT TO SCALE

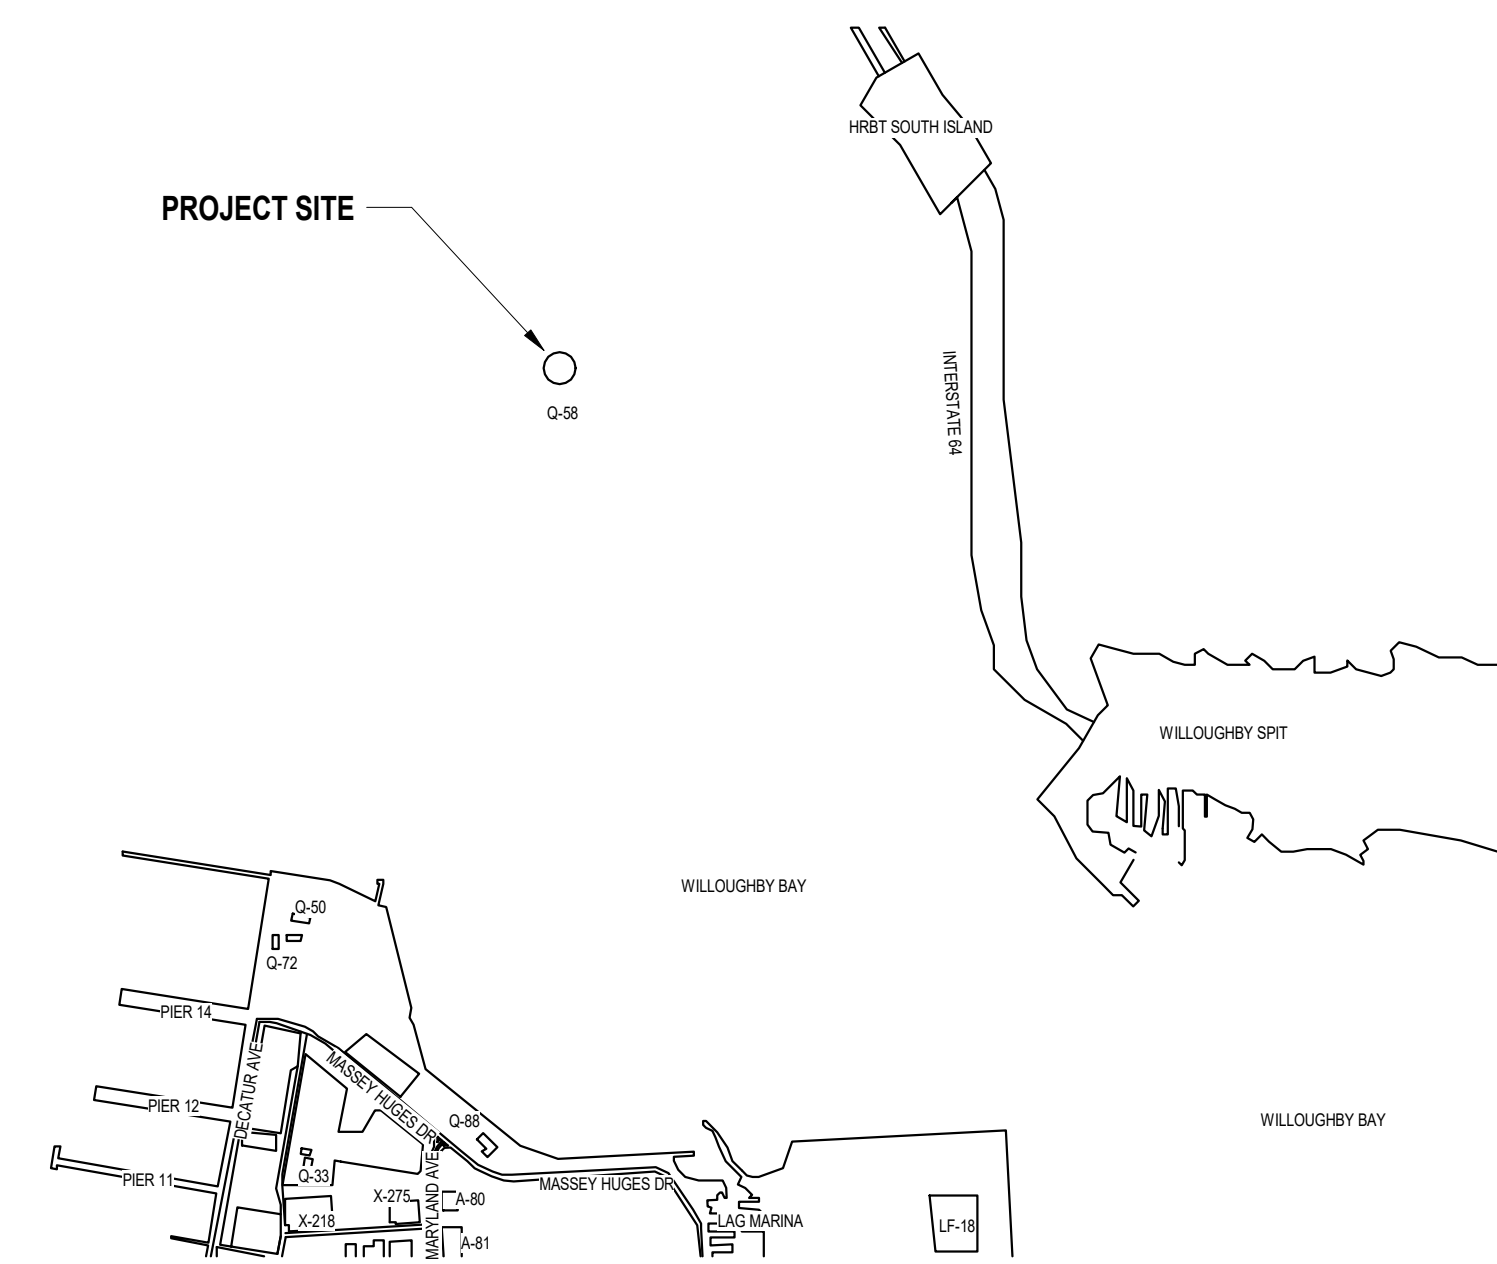

LOCATION MAP  
NOT TO SCALE

## NAVAL FACILITIES ENGINEERING SYSTEMS COMMAND MID-ATLANTIC

ROICC NORFOLK  
FACILITIES ENGINEERING AND ACQUISITION DIVISION  
NORFOLK, VIRGINIA



APPROVED

FOR COMMANDER NAVFAC

ACTIVITY

COMMANDER, NAVY INSTALLATIONS COMMAND

SATISFACTORY TO DATE 01/29/2026

DES ADB DRW ADB CHK DSG

PM/DM DEAN S. GREGORY, P.E.

BRANCH MANAGER JAMES M. SMITH, R.A.

CHIEF ENGINEER JOHN C. MILLER, P.E.

FIRE PROTECTION N/A

NAVAL FACILITIES ENGINEERING SYSTEMS COMMAND

NAVAL FACILITIES ENGINEERING SYSTEMS COMMAND ~ MID-ATLANTIC

NAVAL STATION - NORFOLK, VA

NAVAL STATION NORFOLK

Q-58 DATA CONCENTRATOR SHED RESTORATION

NORFOLK, VIRGINIA

COVER SHEET

SCALE: AS NOTED

PROJECT NO.: 1673784

CONSTR. CONTR. NO. N/A

NAVFAC DRAWING NO. 12.937.903

SHEET 1 OF 5

G-001

DRAWING REVISION: 25 AUGUST 2020


















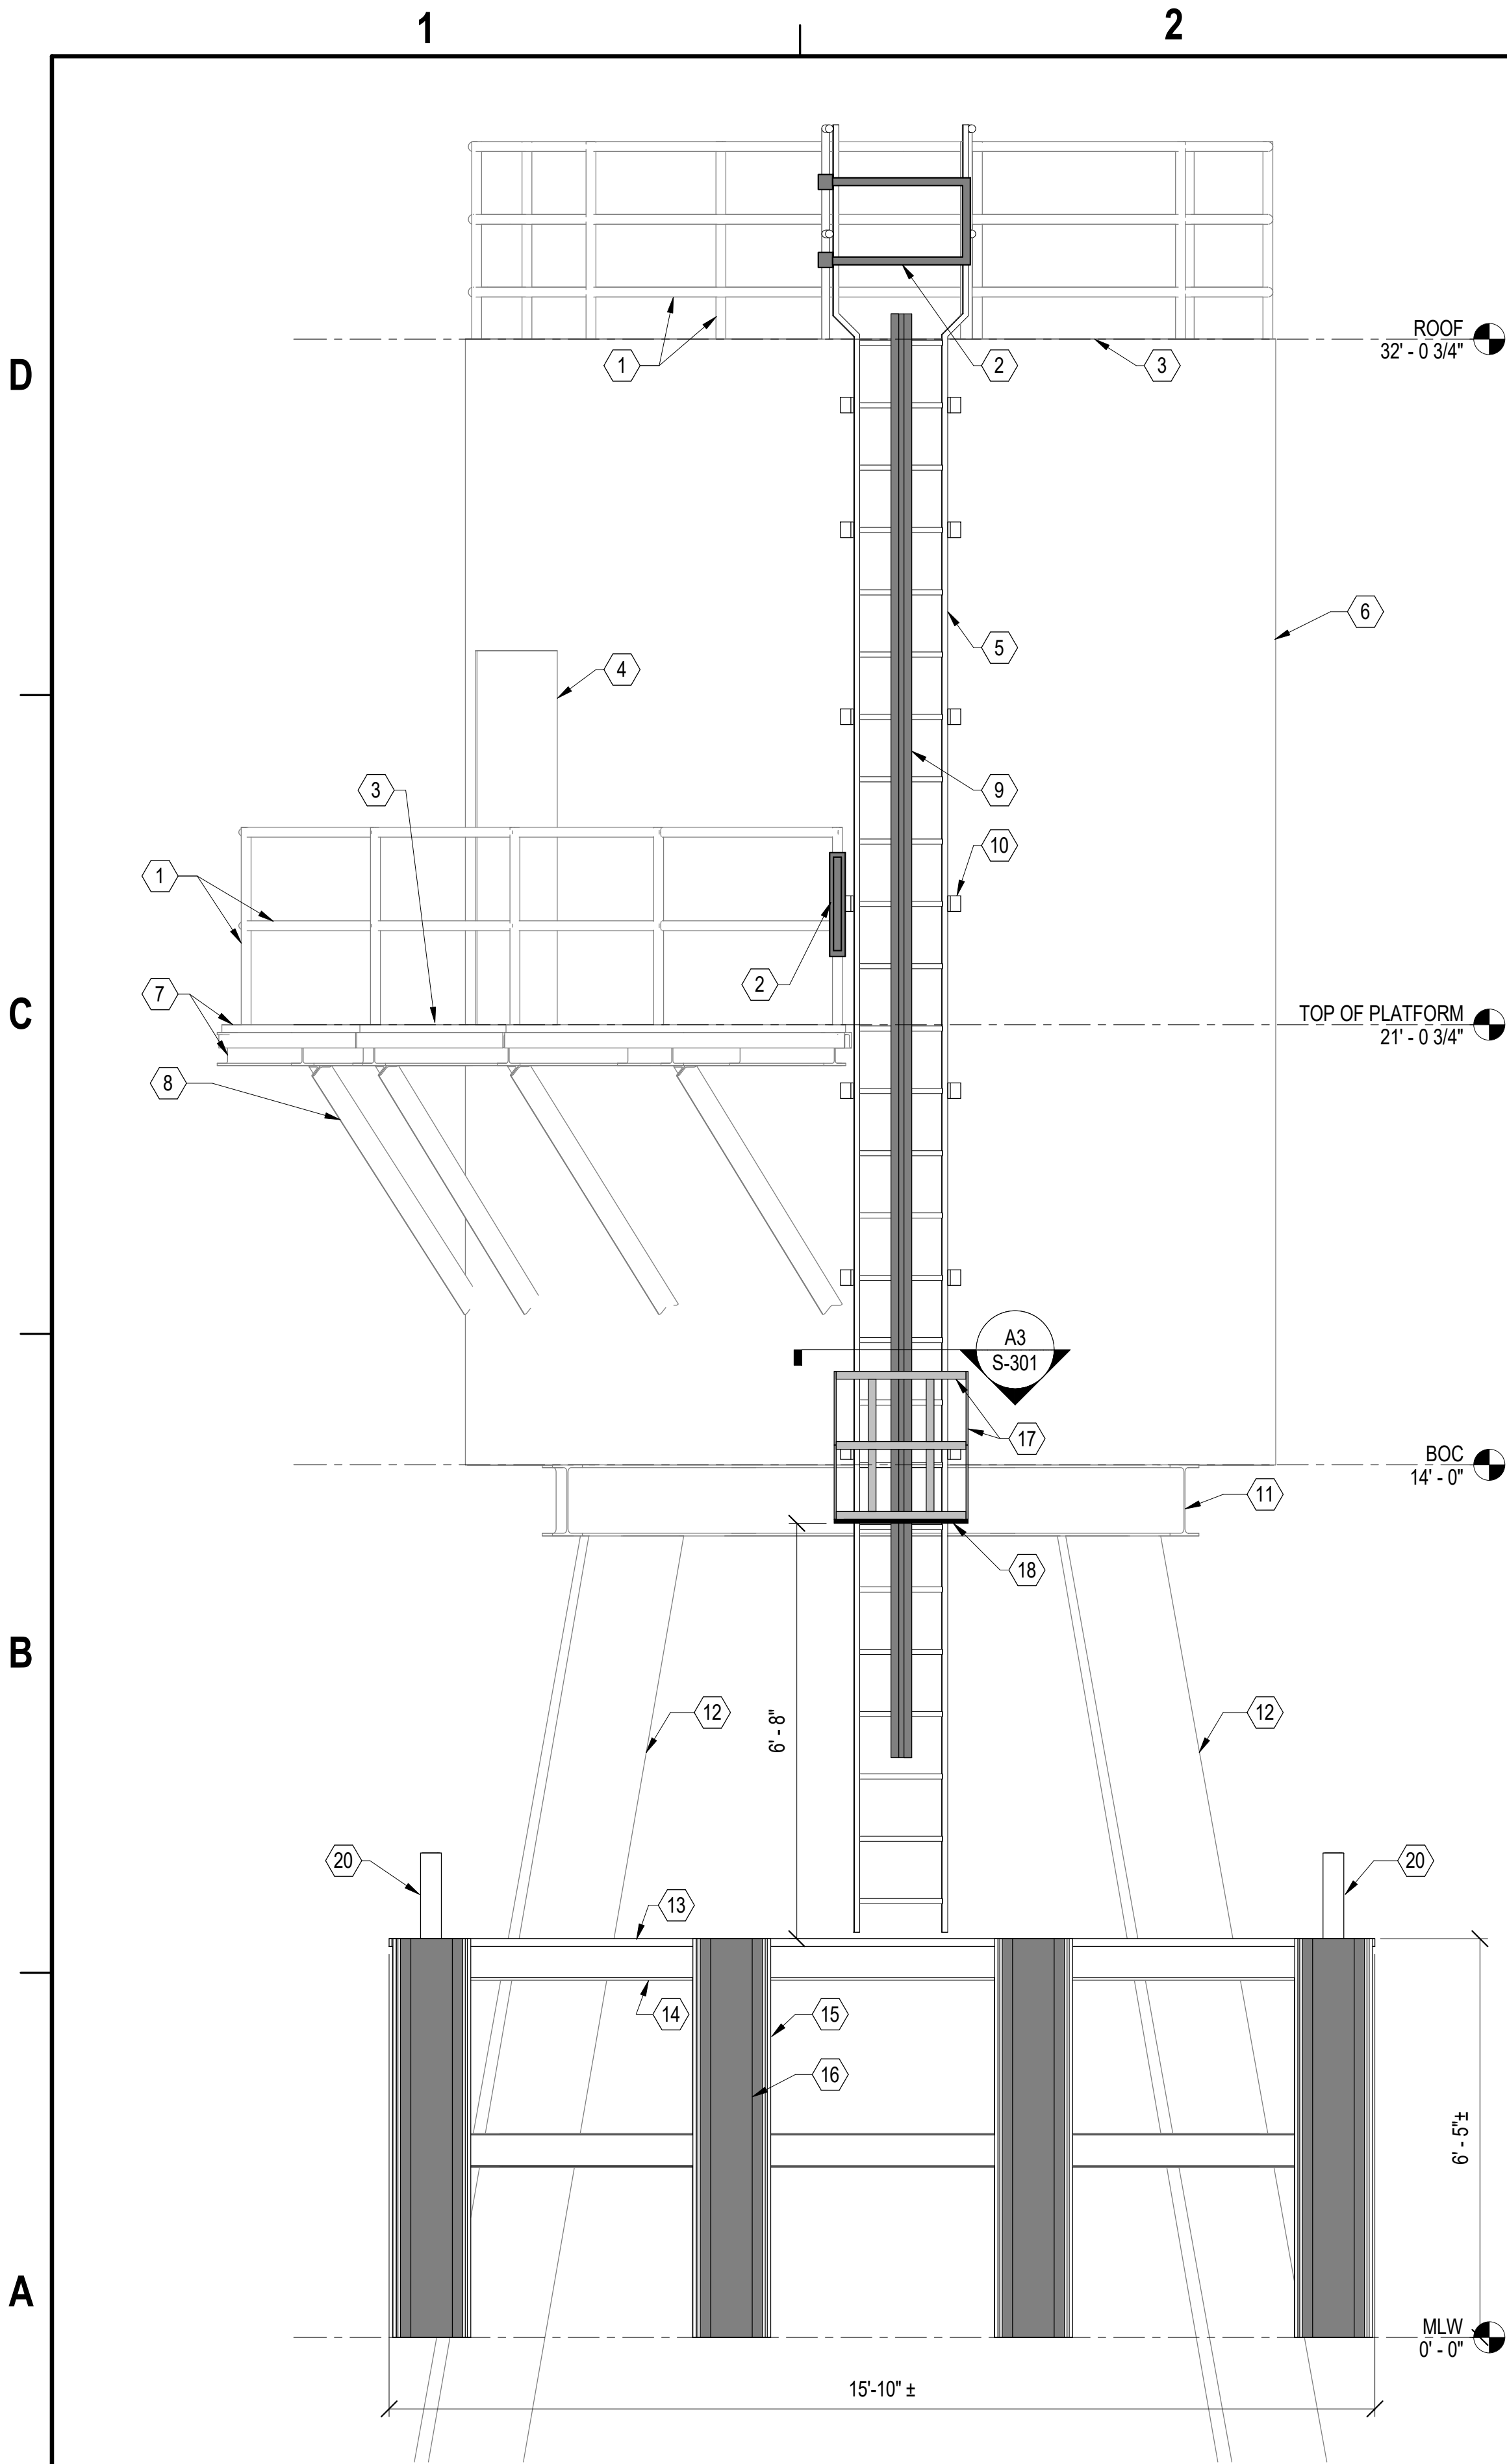

**A1** SOUTH ELEVATION  
1/2" = 1'-0"

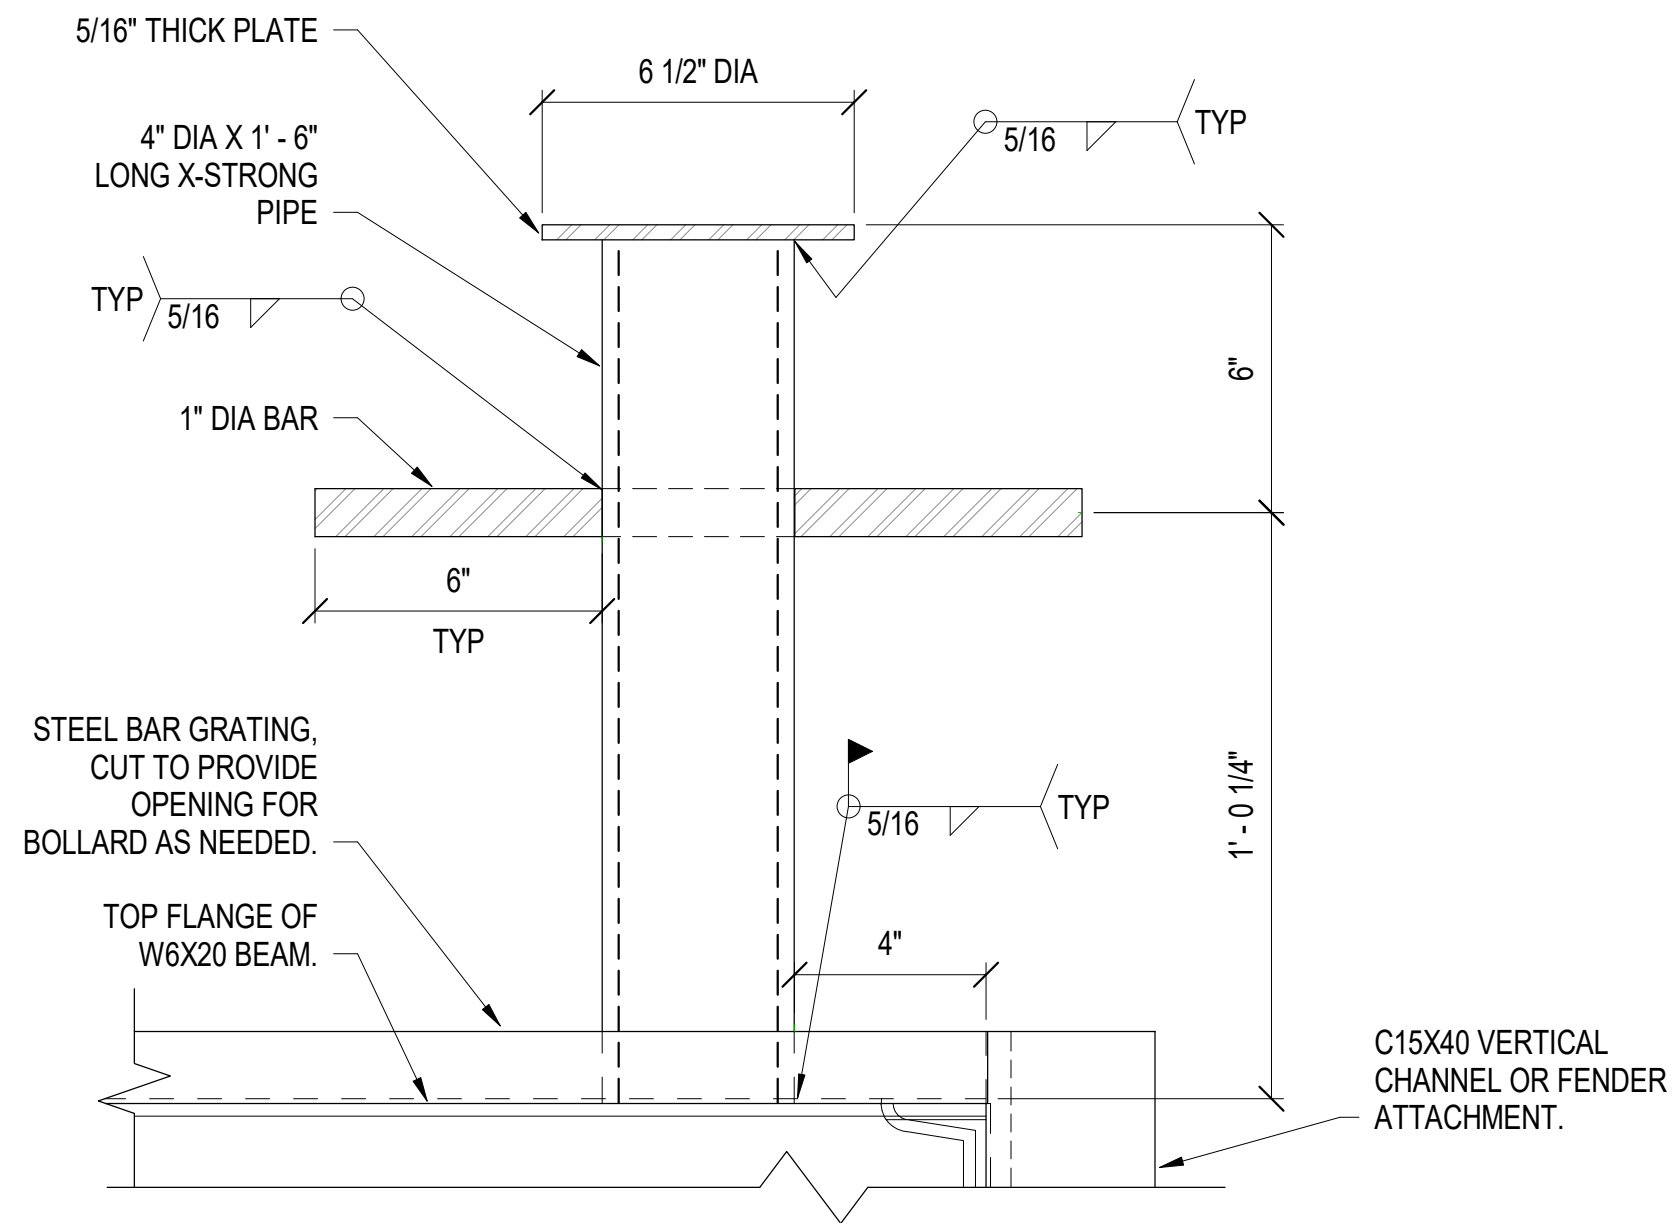

**B3** DETAIL - BOLLARD CONNECTION  
NOT TO SCALE (S-101)

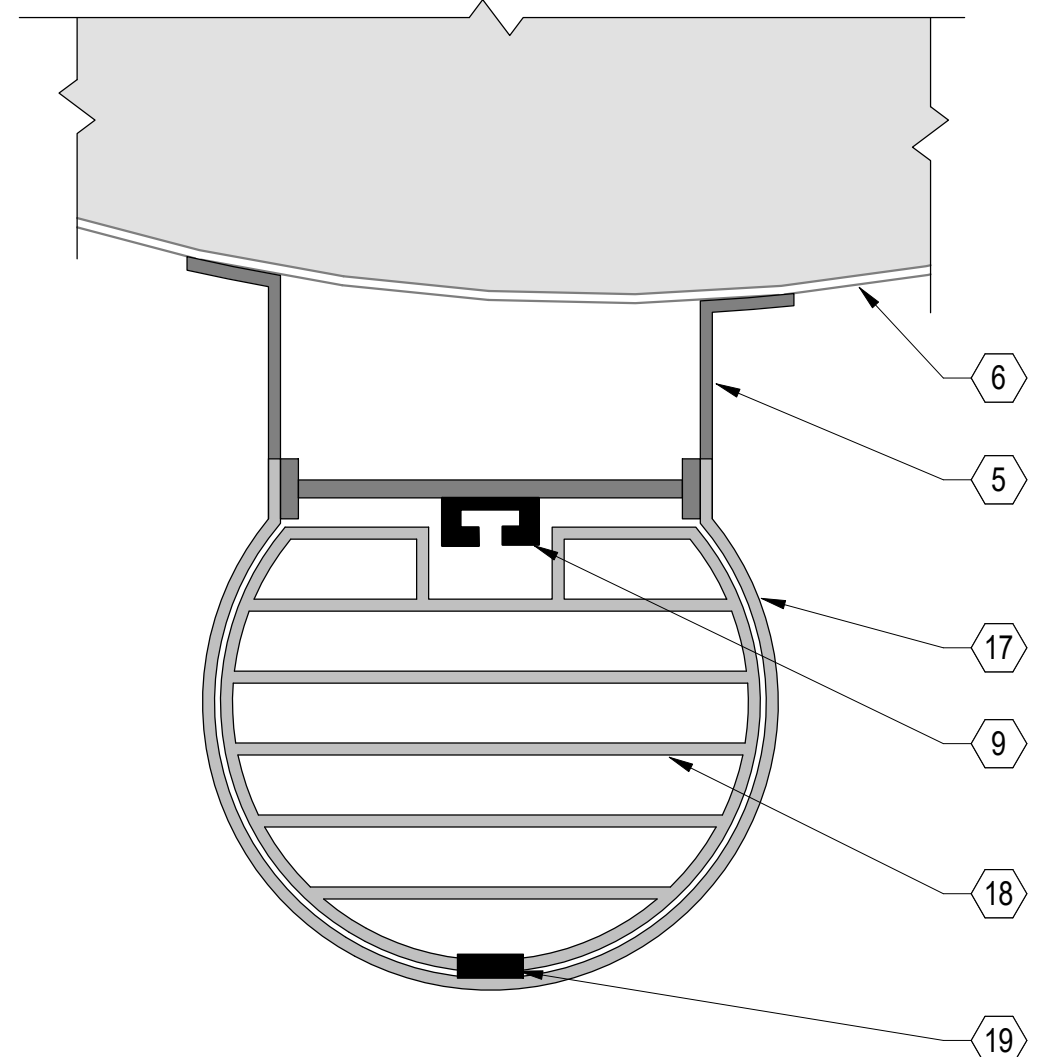

**A3** STEEL SECURITY CAGE AND HATCH  
NOT TO SCALE (S-301)

## GENERAL SHEET NOTES

- 1 THE DATUM ELEVATION FOR THIS DRAWING IS REFERENCING FROM MLW = 0' - 0". THE VERTICAL DISTANCE ABOVE DATUM IS NOTED THUS: X' - X".

## STRUCTURAL KEYNOTES

- 1 EXISTING STEEL PIPE GUARDRAIL, TYP, TO REMAIN.
- 2 PROVIDE METAL SELF-CLOSING SWING GATE IN ACCORDANCE WITH THE 2024 EDITION OF THE DEPARTMENT OF THE NAVY FALL PROTECTION GUIDE. MOUNT TO EXISTING GUARDRAIL POST.
- 3 DEEP CLEAN ROOFTOP SURFACE OF DCS SHELL TO REMOVE BIRD GUANO, BIRD CARCASSES, AND OTHER WASTE MATERIAL. WASTE MUST BE CONSIDERED HAZARDOUS AS BIRD GUANO AND WASTE COULD CARRY DISEASE. COLLECT HAZARDOUS WASTE AND DISPOSE OF IN ACCORDANCE WITH FEDERAL AND LOCAL GUIDANCE. WASTE MUST NOT BE ALLOWED TO ENTER WATERWAY.
- 4 EXISTING STEEL BULKHEAD DOOR TO REMAIN.
- 5 PROVIDE STEEL CLIMBING LADDER IN ACCORDANCE WITH THE 2024 EDITION OF THE DEPARTMENT OF THE NAVY FALL PROTECTION GUIDE. FALL ARREST SYSTEM MUST BE PROVIDED PER LADDER MANUFACTURER.
- 6 EXISTING 3/8" STEEL PLATE SHELL TO REMAIN.
- 7 EXISTING STEEL GRATED AND STEEL FRAMED ACCESS PLATFORM TO REMAIN.
- 8 EXISTING STEEL ANGLE PLATFORM SUPPORT STRUTS, TYP, TO REMAIN.
- 9 PROVIDE FALL ARREST SYSTEM IN ACCORDANCE WITH THE 2024 EDITION OF THE DEPARTMENT OF THE NAVY FALL PROTECTION GUIDE. CONSIDER THE HIGHLY CORROSIVE ENVIRONMENT WHEN SELECTING FALL ARREST SYSTEM HARDWARE.
- 10 ANCHORAGE PER LADDER MANUFACTURER, TYP. FOR BID PURPOSES ASSUME L8X2X3/8" WELDED TO LADDER RAIL AND 3/8" DCS SHELL PLATE, TYP.
- 11 EXISTING STEEL FRAMED PILE CAP. TYP, TO REMAIN.
- 12 EXISTING 18" DIAM., 1/2" THICK STEEL PIPE PILE TO REMAIN.
- 13 PROVIDE STEEL GRATING CAPABLE OF SUPPORTING 150 PSF OVER A 5-FT SPAN. ATTACH TO TOP FLANGE OF NEW CHANNEL BEAMS PER MANUFACTURER'S RECOMMENDATIONS.
- 14 PROVIDE C6X10.5 BEAM, TYP. ATTACH TO ENDS OF W6X20 BEAMS USING CLIP ANGLES AND BOLTS AS SPECIFIED. ENSURE TOS IS FLUSH.
- 15 PROVIDE C15X40 STEEL VERTICAL SUPPORTS FOR FENDER ATTACHMENT, TYP.
- 16 PROVIDE FOAM WING TYPE FENDER WITH MINIMUM OUTSIDE DIAMETER OF 8", TYP.. ATTACHMENT TO C15X40 CHANNEL SUPPORTS PER MANUFACTURER'S INSTRUCTIONS. FOR BIDDING PURPOSES ASSUME 1/2" THICK PLATE STRIP, 1 1/2" WIDE, THROUGH BOLTED INTO C15X40 EVERY 16" O.C.
- 17 PROVIDE PRE-MANUFACTURED STEEL SECURITY CAGE. ATTACH TO NEW LADDER SIDE RAILS.
- 18 PROVIDE PRE-MANUFACTURED STEEL SECURITY HATCH. ATTACH TO STEEL SECURITY CAGE PER MANUFACTURER'S INSTRUCTIONS. HATCH MUST NOT INTERFERE WITH FALL ARREST SYSTEM TRACK OR CABLE.
- 19 SECURITY HATCH HINGE PER MANUFACTURER.
- 20 PROVIDE 4" DIA X 1'-6" X-STRONG PIPE. REFER TO DETAIL B3/S-301 FOR MORE INFORMATION.

| SYN | DESCRIPTION | DATE | APPR |
|-----|-------------|------|------|
|     |             |      |      |
|     |             |      |      |
APPROVED  
FOR COMMANDER NAVFAC  
ACTIVITY  
COMMANDER, NAVY INSTALLATIONS COMMAND

|                                       |     |     |                     |            |     |
|---------------------------------------|-----|-----|---------------------|------------|-----|
| R COMMANDER NAVFAC                    |     |     |                     |            |     |
| TIVITY                                |     |     |                     |            |     |
| COMMANDER, NAVY INSTALLATIONS COMMAND |     |     |                     |            |     |
| TISFACTORY TO DATE                    |     |     |                     | 01/28/2026 |     |
| S                                     | ADB | DRW | ADB                 | CHK        | DSG |
| DM                                    |     |     | DEAN S. GREGORY, P. |            |     |
| RANCH MANAGER                         |     |     | JAMES M. SMITH, R.  |            |     |
| EF ENG/ARCH                           |     |     | JOHN C. MILLER, P.  |            |     |
| E PROTECTION                          |     |     | N                   |            |     |

DEPARTMENT OF THE NAVY  
NAVAL FACILITIES ENGINEERING SYSTEMS COMMAND  
NAVAL FACILITIES ENGINEERING SYSTEMS COMMAND ~ MID-ATLANTIC  
MID-ATLANTIC REGIONAL OFFICE  
NAVAL STATION NORFOLK  
NORFOLK, VIRGINIA  
Q-58 DATA CONCENTRATOR SHED RESTORATION  
SOUTH ELEVATION

|                    |            |
|--------------------|------------|
| SCALE:             | AS NOTED   |
| PROJECT NO.:       | 1673784    |
| CONSTR. CONTR. NO. | N/A        |
| NAVFAC DRAWING NO. | 12.937.907 |
| SHEET              | 5 OF 5     |

S-301

DRAWFORM REVISION: 25 AUGUST 2020