


REVISIONS					
SYMBOL	DESCRIPTION	BY	DATE	APPROVAL	
7	Del. hosp. side lines; Added G.T. School & A School Brooks	AG	02/02		
8	Field changes, removed abnd. services to demo'ed bldgs.	AG	04/03		
9	Field changes, removed abnd. services to demo'ed bldgs.	AG	02/04		
10	Field changes, removed abnd. services to demo'ed bldgs.	AG	09/05		

LEGEND

- | | |
|-------|---------------------------------|
| ———— | UNDERGROUND STEAM RUNS |
| | ABOVEGROUND STEAM RUNS |
| -W-W- | HIGH TEMPERATURE HOT WATER RUNS |
| -W-W- | HIGH TEMPERATURE HOT WATER RUNS |
| HPS | UNDERGROUND STEAM RUNS |
| MPS | ABOVEGROUND STEAM RUNS |
| LPS | HIGH TEMPERATURE HOT WATER RUNS |
| * | PRESSURE REGULATING VALVE |

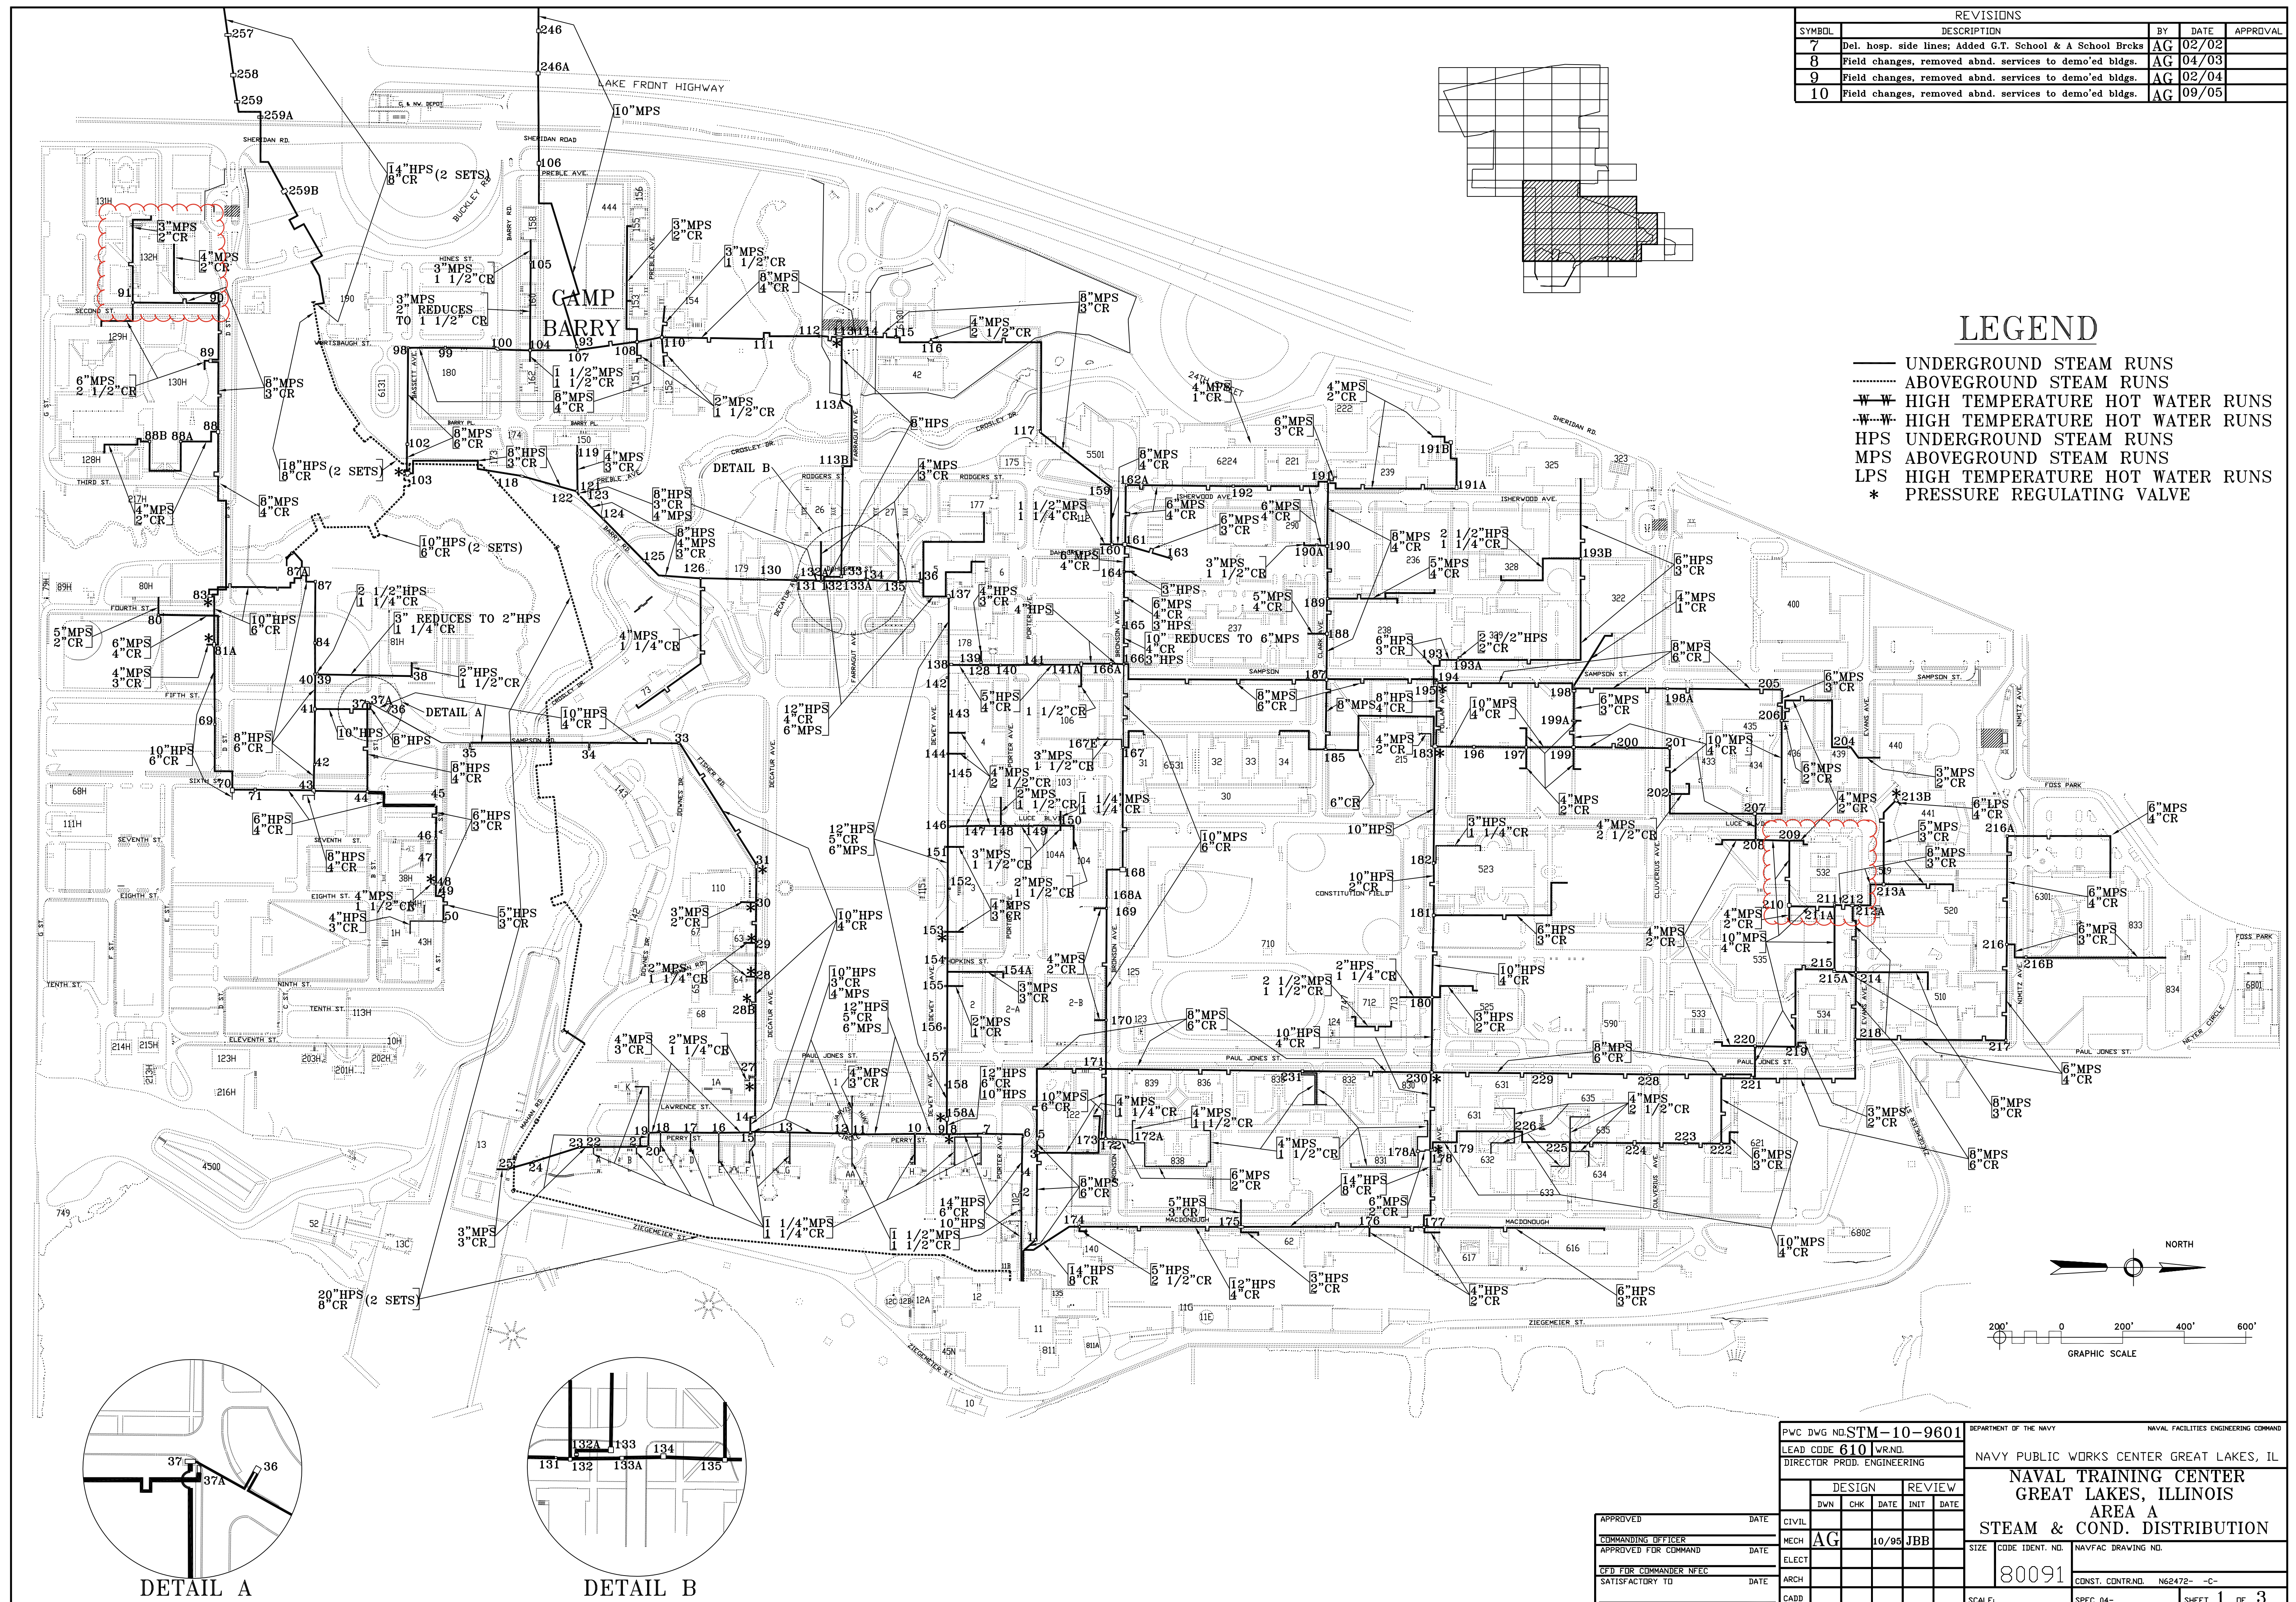

DETAIL A

DETAIL B

PWC DWG NO. STM-10-9601				DEPARTMENT OF THE NAVY				NAVAL FACILITIES ENGINEERING COMMAND			
LEAD CODE 610 WR.ND.				NAVY PUBLIC WORKS CENTER GREAT LAKES, IL							
DIRECTOR PROD. ENGINEERING				NAVAL TRAINING CENTER GREAT LAKES, ILLINOIS AREA A STEAM & COND. DISTRIBUTION							
DESIGN		REVIEW									
	DWN	CHK	DATE	INIT	DATE	SIZE CODE IDENT. NO. NAVFAVC DRAWING NO. 80091 CONST. CONTR. NO. N62472- -C-					
TE	CIVIL										
	MECH	AG	10/95	JBB							
TE	ELECT										
TE	ARCH										
	CADD					SCAL. F.		SPEC. DA-		SHEET 1 OF 3	