
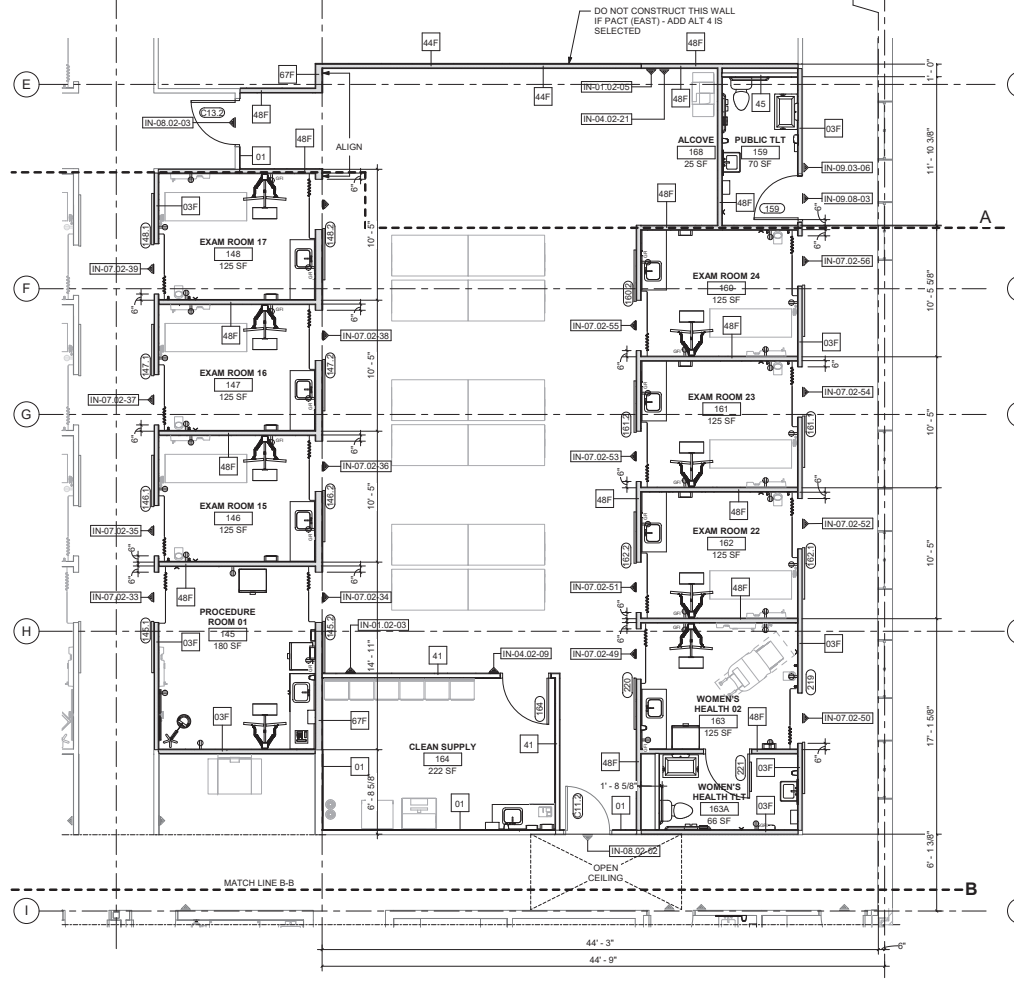


1 ENLARGED FLOOR PLAN - PACT (WEST)
1/4" = 1'-0"

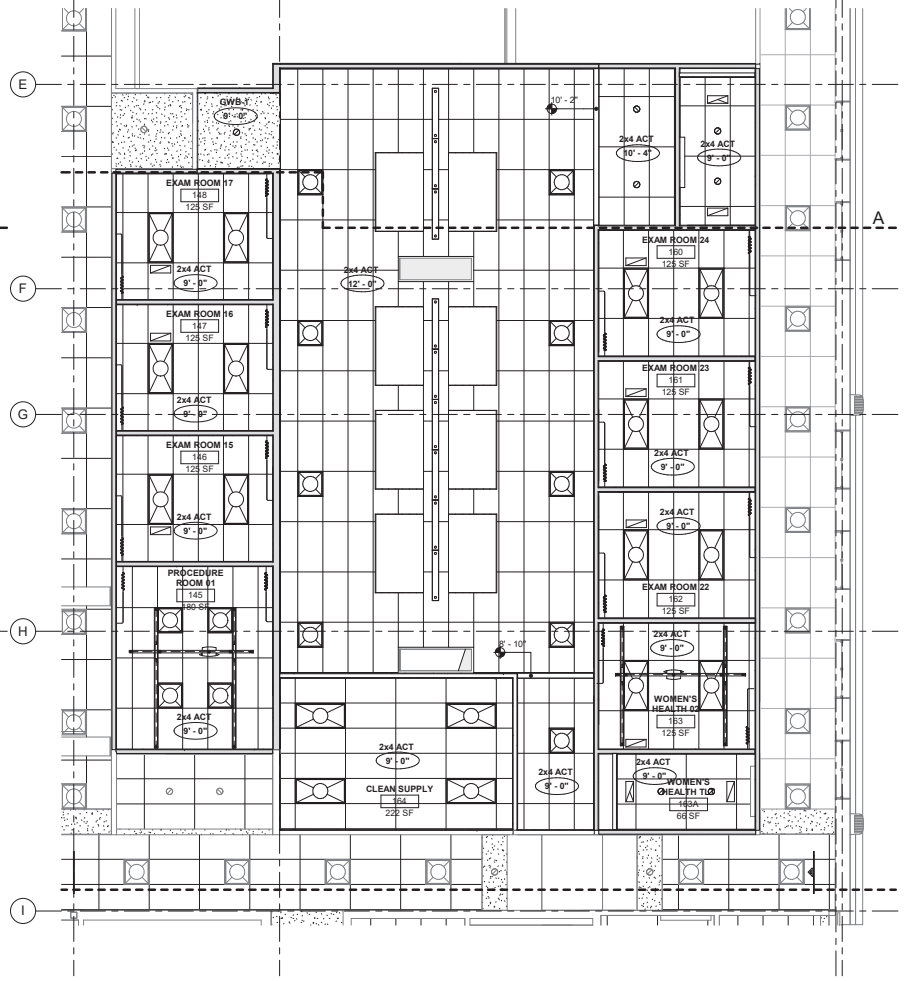

2 ENLARGED REFLECTED CEILING PLAN - PACT (WEST)
1/4" = 1'-0"

GENERAL NOTES

1. ADD ALTERNATE THREE WILL BE CONSTRUCTED IN THE PACT TEAM SHELL WEST AND IS MIRRORED FROM THE PACT TEAM SPACE TO THE EAST. THE DESIGN IS A "U" SHAPED FLOOR PLAN THAT INCLUDES EXAM ROOMS, A PROCEDURE ROOM, A WOMEN'S HEALTH, AND A CLEAN SUPPLY ROOM. EACH EXAM ROOM WILL CONSIST OF TYPICAL EQUIPMENT (SEE SHEET AE452) AND A MAJORITY WILL BE FURNISHED AND INSTALLED BY THE VA AND THE REMAINING BY THE GENERAL CONTRACTOR. PATIENTS WILL UTILIZE THE EXTERIOR CORRIDORS TO ENTER THE EXAM ROOMS AND THE PROVIDERS WILL UTILIZE THE CENTRALIZED INTERIOR ALCOVE. THE CENTRALIZED ALCOVE UTILIZES ACOUSTICAL CANOPIES FOR NOISE REDUCTION THROUGHOUT THE SPACE AND WORKSTATIONS FOR THE PROVIDERS TO WORK SEAMLESSLY IN AND OUT OF THE EXAM ROOMS.
 IF ADD ALTERNATE THREE IS THE ONLY ADD ALTERNATE SELECTED THERE WILL BE A WALL CONSTRUCTED ON THE NORTHERN BORDER TO CUT OFF ACCESS TO THE REST OF THE PACT TEAM SHELL. AS NOTED IN THE DRAWINGS, IF ADD ALTERNATE FOUR IS SELECTED, THE WALL IN THE NORTHERN BORDER OF ADD ALTERNATE FOUR WILL NOT BE CONSTRUCTED. REFER TO THE NOTE LOCATED ON AE452. "DO NOT CONSTRUCT THIS WALL IF PACT (EAST) – ADD ALT 4 IS SELECTED"
2. REFERENCE SPEC 01 00 00 GENERAL REQUIREMENTS FOR MORE INFORMATION.

Revisions:	Date:

CONSULTANT

ARCHITECT/ENGINEER OF RECORD

A/E:
SPEES DESIGN BUILD
625 1ST AVE #301
SEATTLE, WA, 98014
(206) 590-2118
RAY SPEES, PRESIDENT

SDB SPEESDESIGNBUILD

STAMP

10000 REGISTERED ARCHITECT JAMES M. KING STATE OF WASHINGTON

Office of Construction and Facilities Management

VA U.S. Department of Veterans Affairs

Drawing Title PACT (WEST) - ADD ALT 3	**Phase** CONSTRUCTION DOCUMENTS	**Project Title** CONSTRUCT PRIMARY CARE / MENTAL HEALTH BUILDING	**Project Number** 531-325
			Building Number 127
Approved: MEDICAL CENTER DIRECTOR		**Location** BOISE VA MEDICAL CENTER - BOISE, ID	**Drawing Number** AE452
Approved: CHIEF, FACILITY MANAGEMENT SERVICE		**Issue Date** 07/23/2021 **Checked** MK **Drawn** MA	**086 OF 206**

VA FORM 08 - 6231