


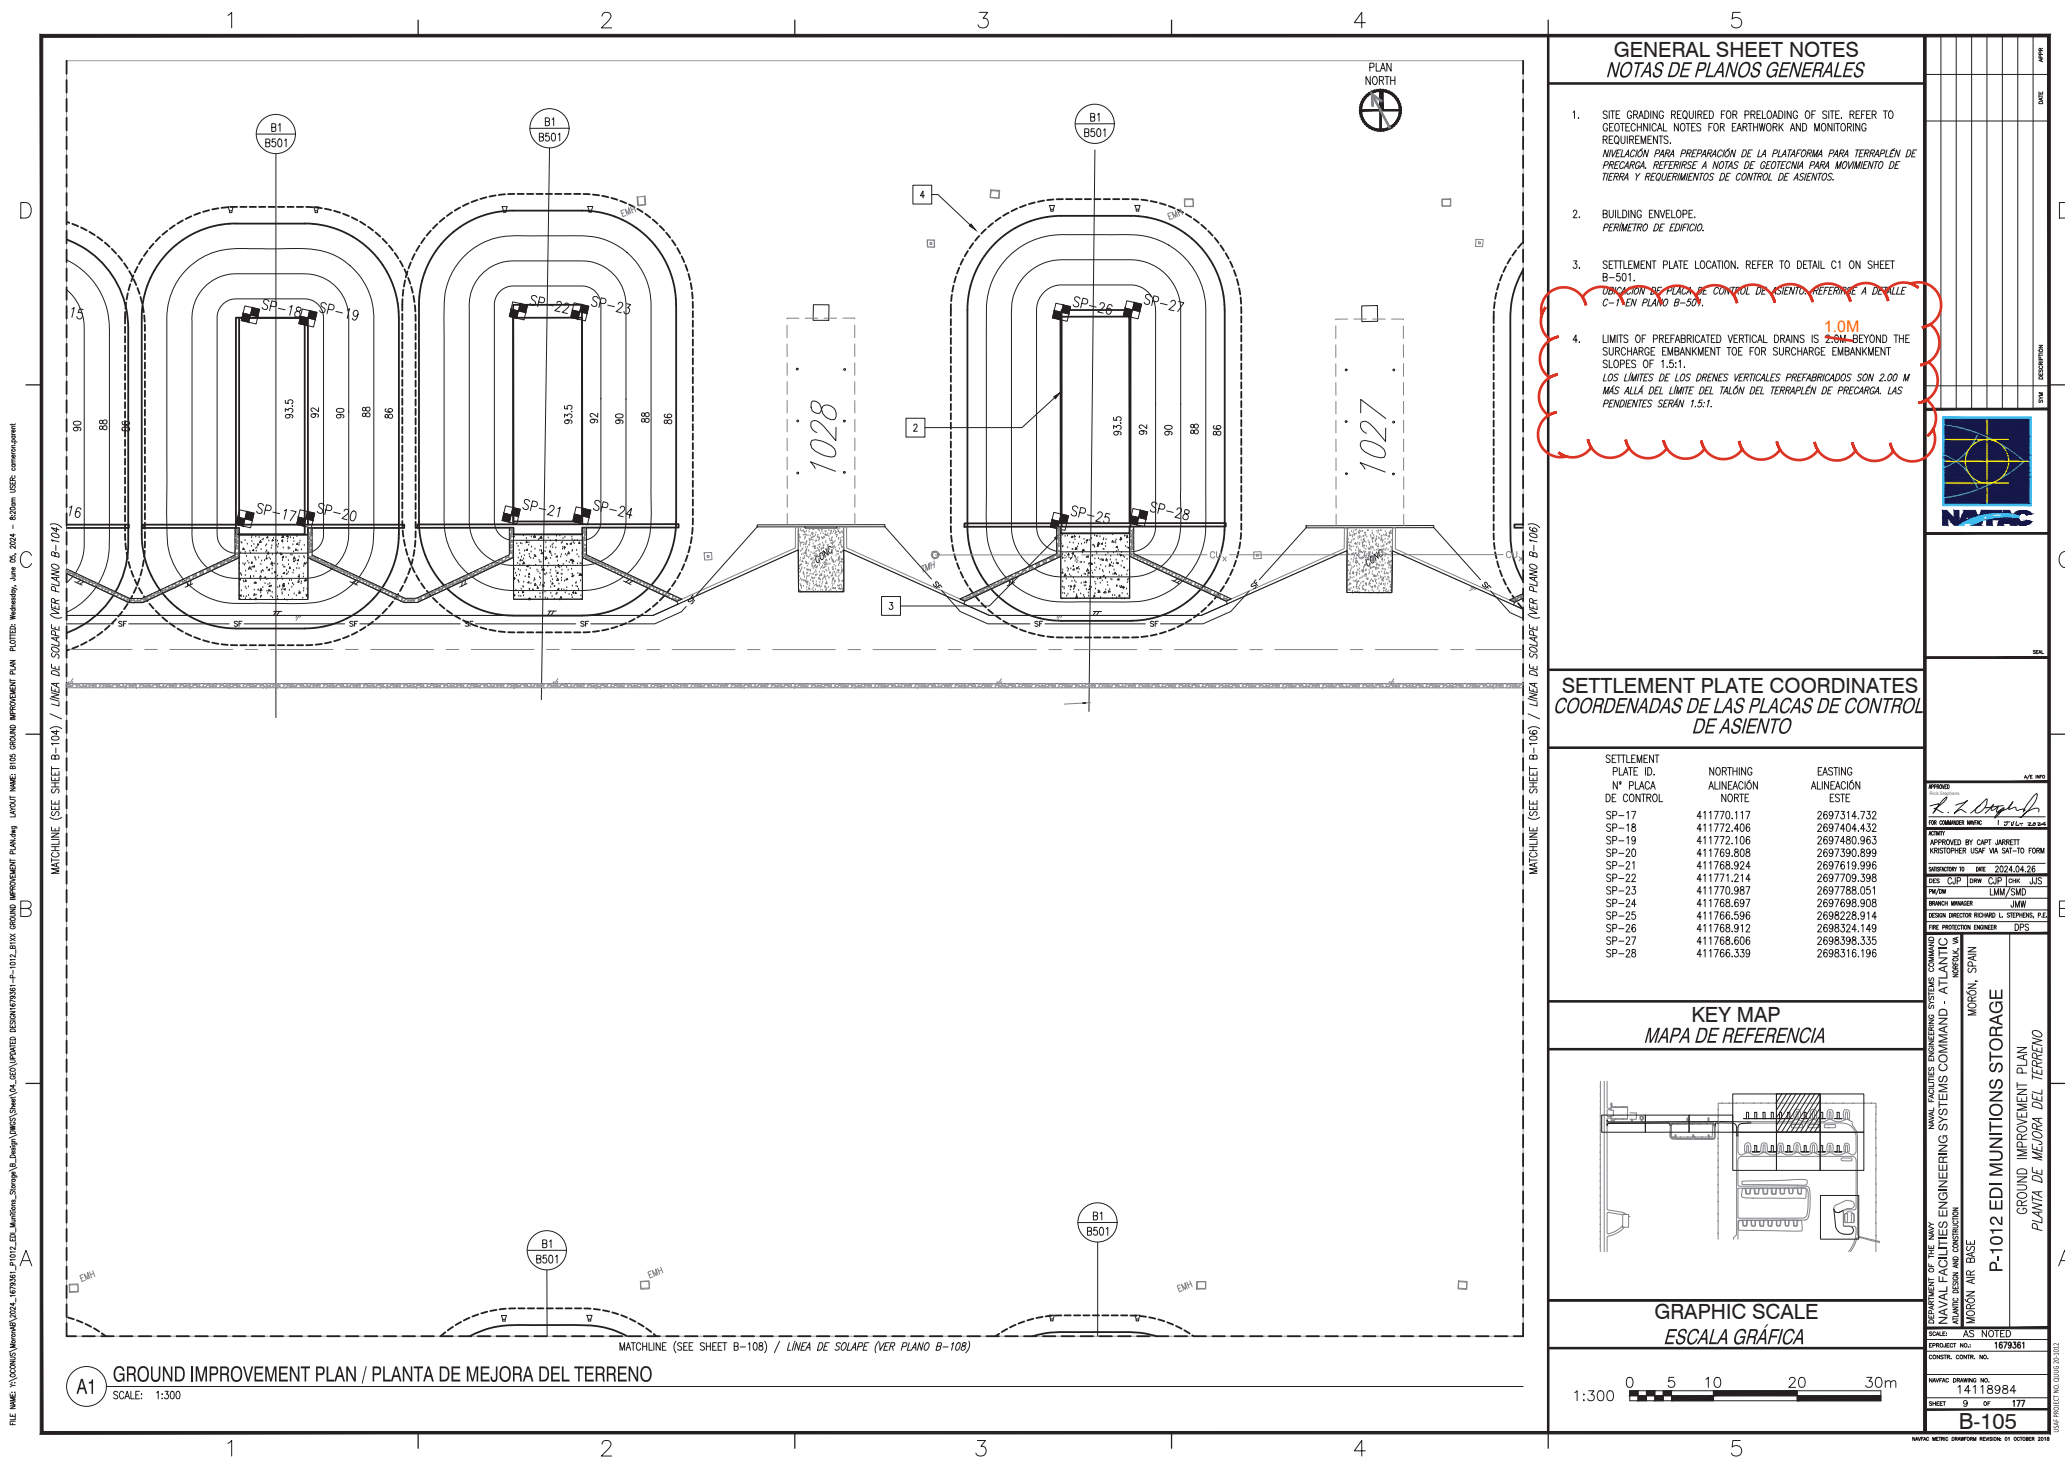

GENERAL SHEET NOTES
NOTAS DE PLANOS GENERALES

1. SITE GRADING REQUIRED FOR PRELOADING OF SITE. REFER TO GEOTECHNICAL NOTES FOR EARTHWORK AND MONITORING REQUIREMENTS.
NIVELACIÓN PARA PREPARACIÓN DE LA PLATAFORMA PARA TERRAPLEN DE TIERRA. REFERIRSE A NOTAS DE GEOTECNIA PARA MOVIMIENTO DE TIERRA Y REQUERIMIENTOS DE CONTROL DE ASIENTOS.
2. BUILDING ENVELOPE.
PERIMETRO DE EDIFICIO.
3. SETTLEMENT PLATE LOCATION. REFER TO DETAIL C1 ON SHEET B-501.
UBICACIÓN DE PLACA DE CONTROL DE ASIENTO. REFERIRSE A DETALLE C-1 EN PLANO B-501.
4. LIMITS OF PREFABRICATED VERTICAL DRAINS IS 2.0M BEYOND THE SURCHARGE EMBANKMENT TOE FOR SURCHARGE EMBANKMENT SLOPES OF 1:5:1.
LOS LÍMITES DE LOS DREÑES VERTICALES PREFABRICADOS SON 2.00 M MÁS ALLA DEL LÍMITE DEL TALÓN DEL TERRAPLEN DE PRECARGA. LAS PENDIENTES SERÁN 1:5:1.



SETTLEMENT PLATE COORDINATES COORDENADAS DE LAS PLACAS DE CONTROL DE ASIENTO


SETTLEMENT PLATE ID. N° PLACA DE CONTROL	NORTHING ALINEACIÓN NORTE	EASTING ALINEACIÓN ESTE
SP-17	411770.117	2697314.732
SP-18	411772.406	2697404.432
SP-19	411772.106	2697480.963
SP-20	411768.808	2697390.899
SP-21	411768.924	2697619.996
SP-22	411771.214	2697709.398
SP-23	411770.987	2697788.051
SP-24	411768.697	2697628.908
SP-25	411766.596	2698228.914
SP-26	411766.912	2698314.149
SP-27	411768.606	2698396.335
SP-28	411766.339	2698316.196

APPROVED A/E INFO
 (Signature)

 FOR COMMANDER INFO: 1 JUL 2004
 ACTIVITY
 APPROVED BY CAPT JARRETT
 KRISTOPHER USAF WA SAT-TO FORM

 SATISFACTORY TO DATE 2024.04.26
 DES CJP DRW CJP CHK JJS
 PM/DW LMM/SMD
 BRANCH MANAGER JMW
 (Signature)
 DESIGN DIRECTOR RICHARD L STEPHENS, P.E.
 FIRE PROTECTION ENGINEER DPS


KEY MAP
MAPA DE REFERENCIA

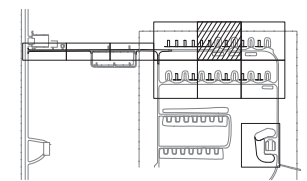

GRAPHIC SCALE
ESCALA GRÁFICA



MORON AIR BASE MORON, SPAIN	
P-1012 EID MUNITIONS STORAGE	
GROUND IMPROVEMENT PLAN PLANTA DE MEJORA DEL TERRENO	
NAVAJA FACILITIES ENGINEERING SYSTEMS COMMAND - AT AVIATION DESIGN AND CONSTRUCTION 1411 1384 SHEET 9 OF 177	
B-105	

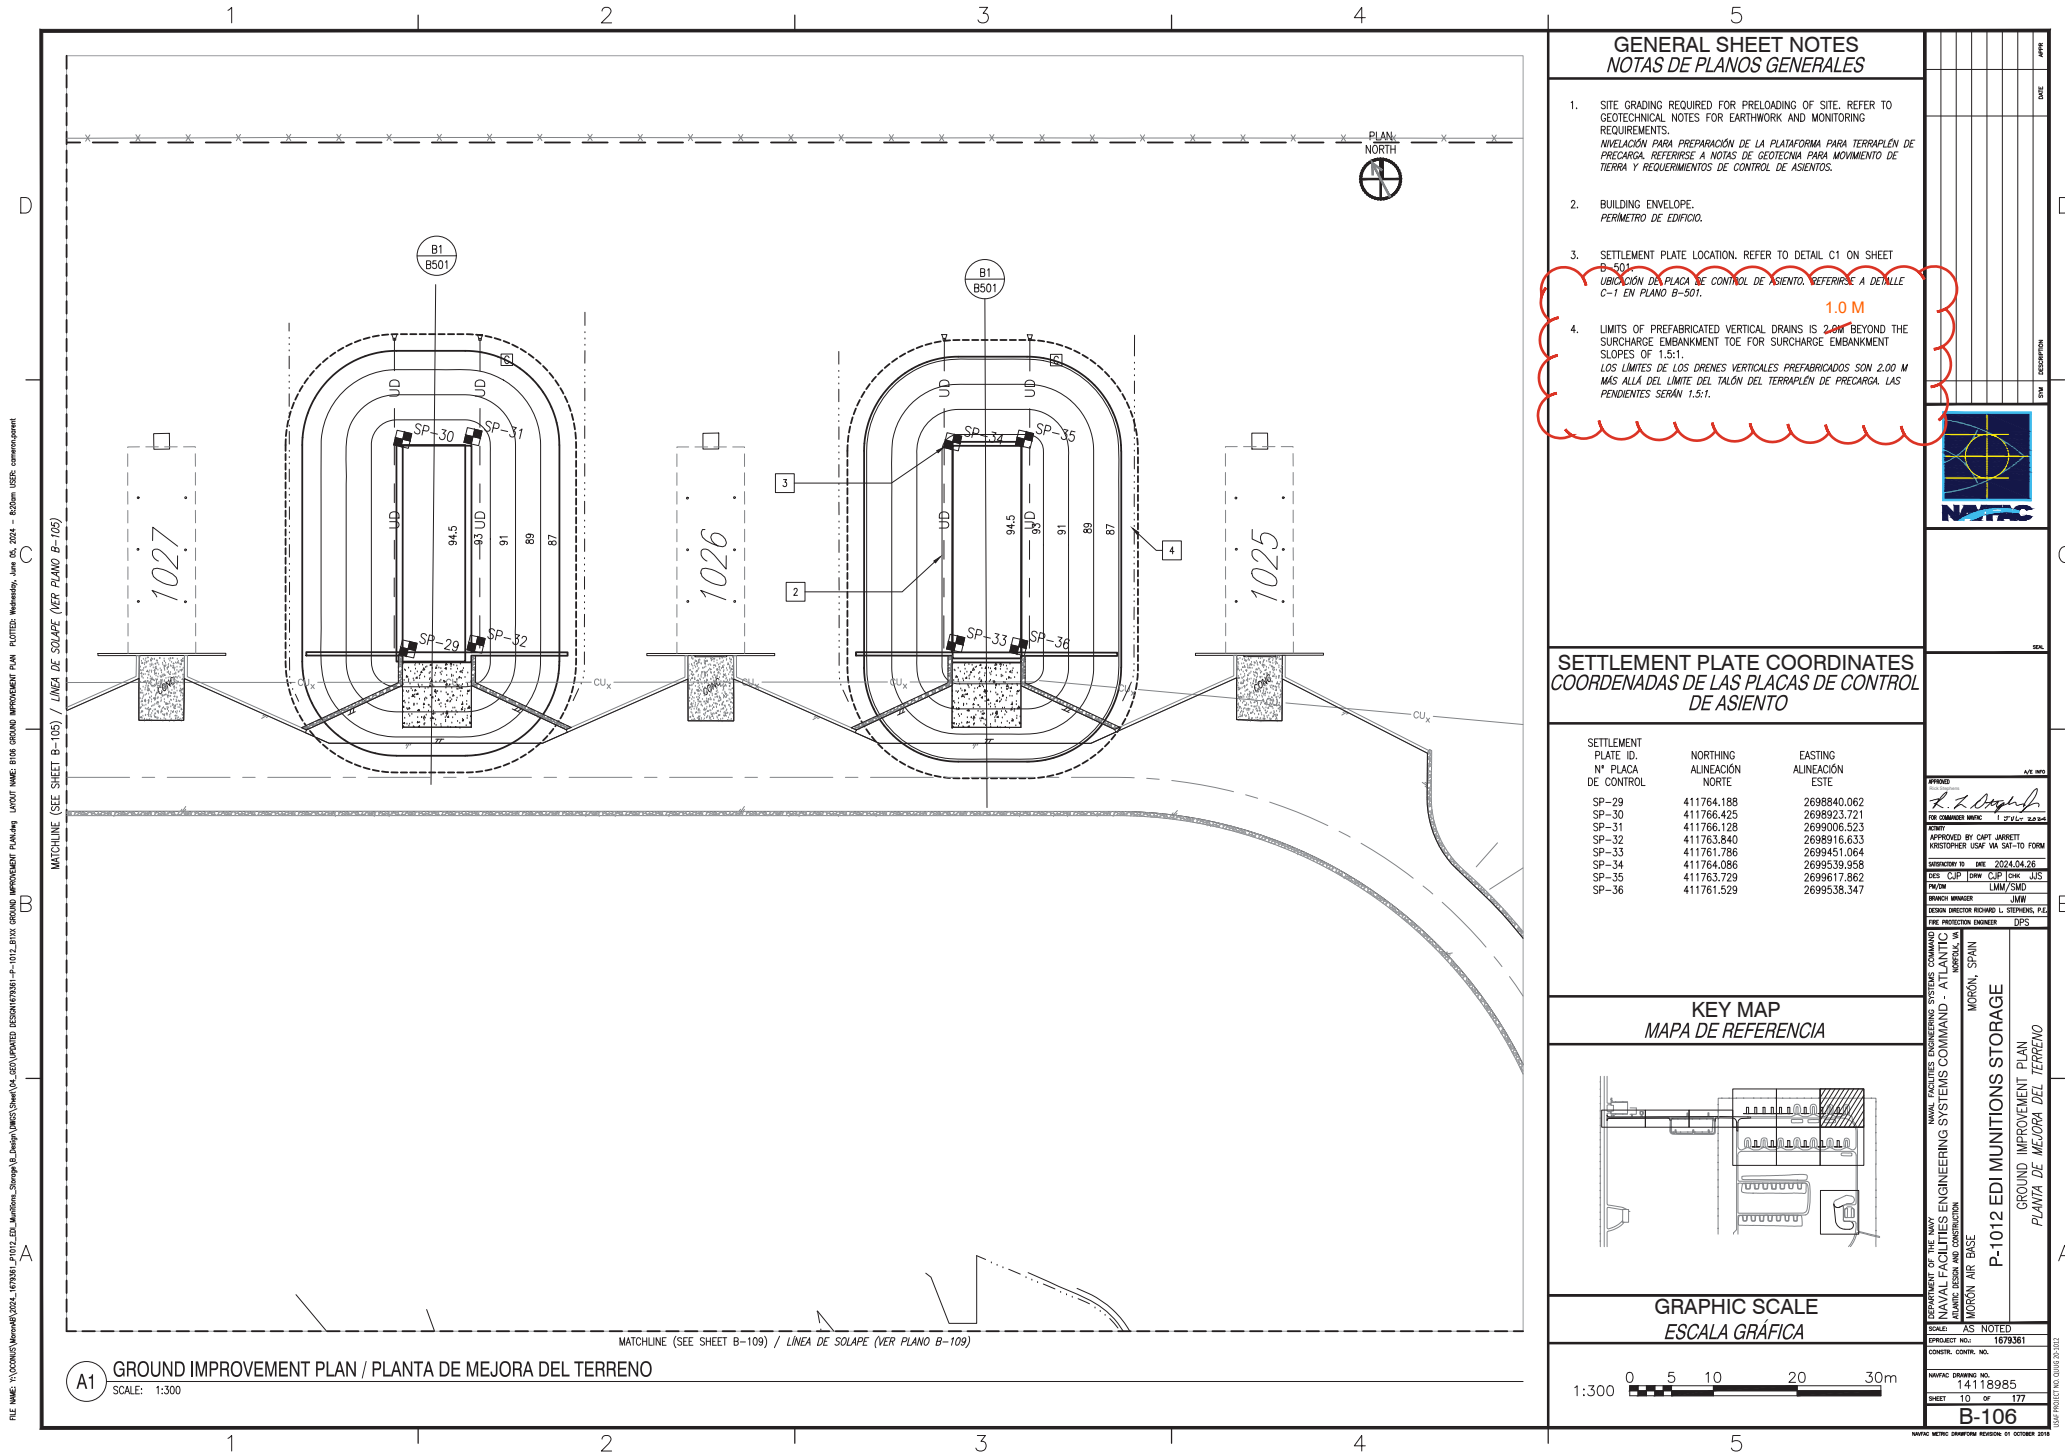


GENERAL SHEET NOTES
NOTAS DE PLANOS GENERALES

1. SITE GRADING REQUIRED FOR PRELOADING OF SITE. REFER TO GEOTECHNICAL NOTES FOR EARTHWORK AND MONITORING REQUIREMENTS.
NIVELACION PARA PREPARACION DE LA PLATAFORMA PARA TERRAPLEN DE PRECARGA. REFERIRSE A NOTAS DE GEOTECNIA PARA MOVIMIENTO DE TIERRA Y REQUERIMIENTOS DE CONTROL DE ASIENTOS.
2. BUILDING ENVELOPE.
PERIMETRO DE EDIFICIO.
3. SETTLEMENT PLATE LOCATION. REFER TO DETAIL C1 ON SHEET B-501.
UBICACION DE PLACA DE CONTROL DE ASIENTO. REFERIRSE A DETALLE C-1 EN PLANO B-501.
4. LIMITS OF PREFABRICATED VERTICAL DRAINS IS ~~2.0M~~ *1.0 M* BEYOND THE SURCHARGE EMBANKMENT TOE FOR SURCHARGE EMBANKMENT SLOPES OF 1:5:1.
LOS LIMITES DE LOS DREÑES VERTICALES PREFABRICADOS SON 2.00 M MÁS ALLA DEL LIMITE DEL TALÓN DEL TERRAPLEN DE PRECARGA. LAS PENDIENTES SERÁN 1:5:1.

SETTLEMENT PLATE COORDINATES
COORDENADAS DE LAS PLACAS DE CONTROL
DE ASIENTO

SETTLEMENT PLATE ID. N° PLACA DE CONTROL	NORTHING ALINEACIÓN NORTE	EASTING ALINEACIÓN ESTE
SP-29	411764.188	269880.062
SP-30	411766.425	269893.721
SP-31	411766.128	269906.523
SP-32	411763.840	269891.633
SP-33	411761.786	269945.164
SP-34	411764.086	269953.958
SP-35	411763.729	2699617.862
SP-36	411761.529	2699538.347

KEY MAP
MAPA DE REFERENCIA

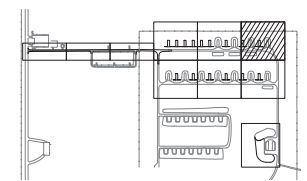

GRAPHIC SCALE
ESCALA GRÁFICA

[illegible]

