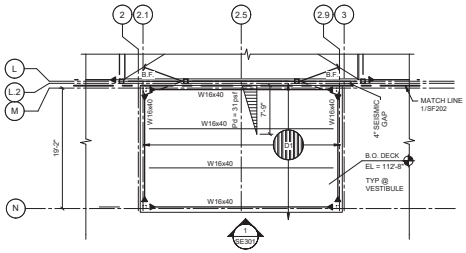

2 VESTIBULE PARTIAL FRAMING PLAN
1/8" = 1'-0"

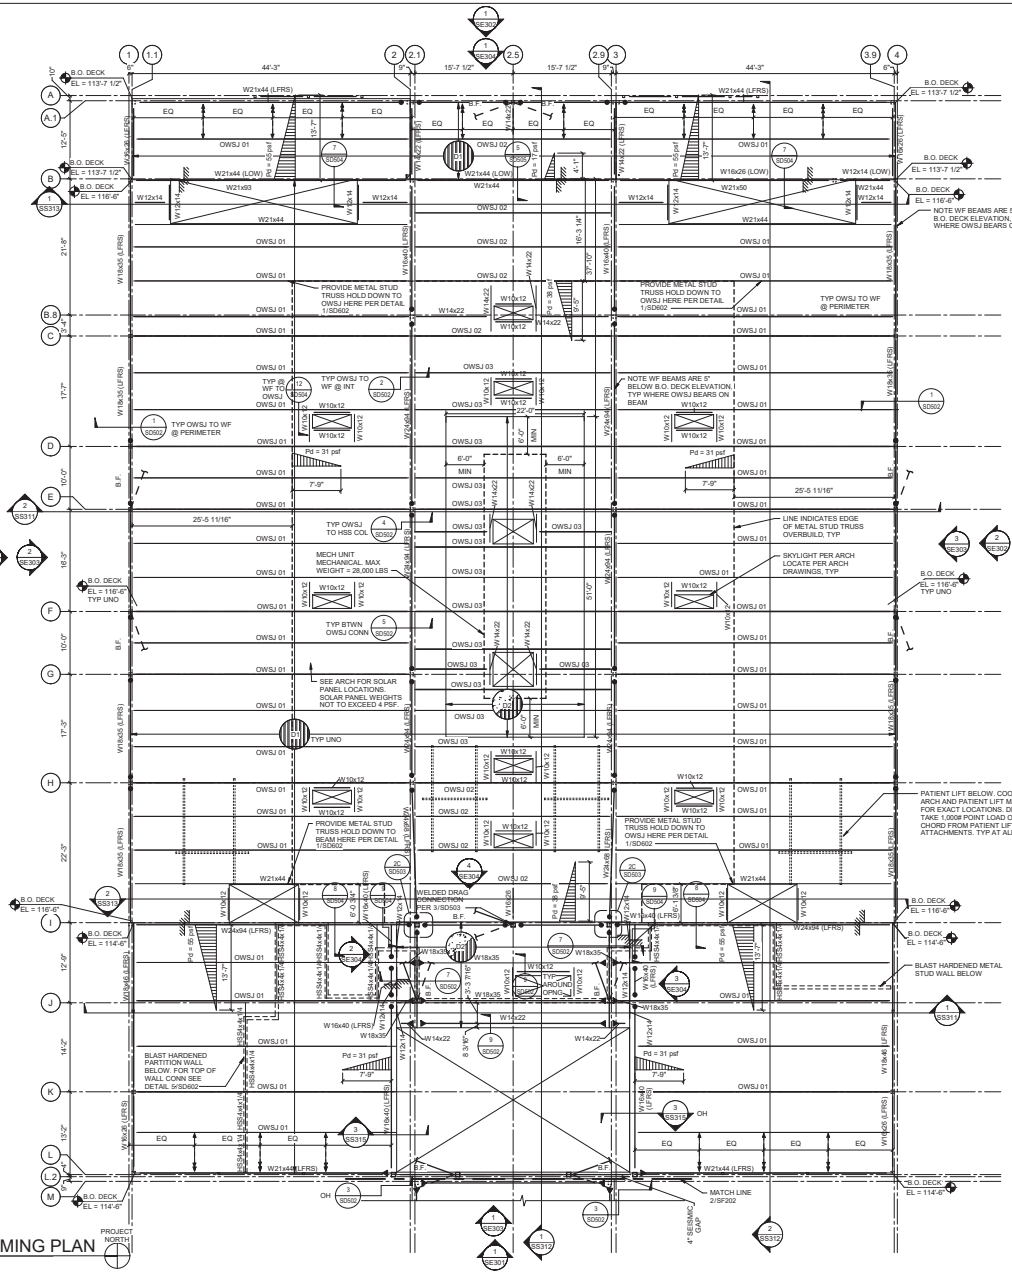

1 FLAT ROOF FRAMING PLAN
1/8" = 1'-0"

FRAMING PLAN NOTES

1. FOR TYPICAL STEEL DETAILS SEE SHEETS SD501,SD502 & SD503
2. INDICATES FRAME BRACE PER ELEVATION.
   INDICATES FRAME BRACE BELOW PER ELEVATION.
3. LFRS — INDICATES THAT THE MEMBER IS PART OF THE LATERAL FORCE RESISTING SYSTEM. SEE 1/SD501 FOR MORE INFORMATION, INCLUDING REQUIREMENTS FOR SLIP CRITICAL BOLTS.
4. FOR METAL STUD WALL FRAMING INCLUDING HEADERS, JAMBS AND SILLS SEE DETAIL 1/SD601
5. B.O. DECK EL = X'-X" — INDICATES BOTTOM OF DECK ELEVATION RELATIVE TO TOP OF SLAB ON GRADE ELEVATION
6. INDICATES DECK TYPE AND SPAN DIRECTION PER 1/SD510 ALL ROOF DECKS FLAT (NO SLOPE) UNLESS NOTED OTHERWISE
7. INDICATES BOTTOM FLANGE BRACE PER DETAIL 6/SD501
8. B.F. — INDICATES BRACE FRAME PER ELEVATION
9. INDICATES TYPICAL DRAG CONNECTION TO HSS PER 2/SD503
10. INDICATES WIDE FLANGE BEAM TO OWSJ DRAG CONNECTION PER DETAIL 6/SD502
11. FOR TYPICAL DECK DETAILS SEE SHEETS SD510
12. INDICATES BEAM TO BEAM MOMENT CONNECTION PER 8/SD502
13. INDICATES WIDE FLANGE BEAM TO HSS COLUMN MOMENT CONNECTION PER 10/SD504
14. Pd = X psf, DIM — INDICATES SNOW DRIFT LOADING AMOUNT AND LENGTH. SEE GENERAL NOTES FOR ADDITIONAL LOADING INFORMATION TO OPEN WEB STEEL JOISTS.
15. OWSJ 0X — INDICATES OPEN WEB STEEL JOISTS PER SCHEDULE IN GENERAL NOTES ON SHEET S-001 .

Revisions:	Date:

CONSULTANT

kpff
412 E. Park Center Blvd, Suite 200
Boise, ID 83706
O: 208.336.6985
www.kpff.com

ARCHITECT/ENGINEER OF RECORD

A/E:
SPEES DESIGN BUILD
625 1ST AVE #301
SEATTLE, WA, 98014
(360) 223 - 8994
RAY SPEES, PRESIDENT

SPEES DESIGN BUILD

STAMP

REGISTERED PROFESSIONAL ENGINEER 12033 STATE OF IDAHO JOHN M. BILLS

Office of Construction and Facilities Management

VA U.S. Department of Veterans Affairs

Drawing Title FLAT ROOF PLAN	**Phase** CONSTRUCTION DOCUMENTS
Approved: MEDICAL CENTER DIRECTOR	
Approved: CHIEF, FACILITY MANAGEMENT SERVICE	

Project Title CONSTRUCT PRIMARY CARE / MENTAL HEALTH BUILDING		**Project Number** 531-325
		Building Number 127
Location BOISE VA MEDICAL CENTER - BOISE, ID		**Drawing Number** SF202
Issue Date 07/23/2021	**Checked** CH/JW / **Drawn** SG	**028 OF 206**

VA FORM 08 - 6231