




GENERAL NOTES:


- A. ALL SUSPENDED ACoustICAL CeILINGS SHALL BE 9'-0" ABOVE FINISH FLOOR UNLESS NOTED OTHERWISE.
- B. LIGHT FIXTURES, CIRCUITS, DIFFUSERS, ETC. ARE SHOWN FOR GENERAL INFORMATION ONLY. COORDINATE WITH THE MECHANICAL AND ELECTRICAL DRAWINGS.
- C. ALL CeILING UNtED EQUIPMENT SHALL BE LOCATED SQUARE AND SYMMETRICAL TO ADJACENT COMPONENTS OR CONSTRUCTION UNLESS NOTED OTHERWISE.
- D. REFER TO FINISH SCHEDULE FOR ALL OYSPUM BOARD SURFACES.
- E. WHERE ACoustICAL CeILINGS OCCUR, ALL FIRE SPRINKLER HEADS SHALL BE CENTERED IN THE TILe UNLESS OTHERWISE INSTRUCTED BY CODE.
- F. THE CeILING SPACE FROM THE BOTTOM OF THE CeILING GRID TO A MINIMUM OF 9' ABOVE THE BOTTOM OF THE CeILING GRID IS TO BE RESERVED FOR INSTALLATION OF CeILING UNtED ITEMS (I.E. LIGHT FIXTURES, SPEAKERS, DIFFUSERS, ETC.). NO PIPING, DUCTWORK, OR OTHER UNtED ITEMS ARE ALLOWED TO BE INSTALLED IN THE SPACE UNLESS OTHERWISE APPROVED BY THE COTR.
- G. ALL WALL ASSEMBLIES TO EXTEND TO STRUCTURAL DECK ABOVE UNO.

~~\$\$\$~~ SHEET NOTES:


1. PATIENT LIFT TRACK- PRIMARY FIXED RAIL. PENDANT MOUNT TO STRUCTURE ABOVE.
2. PATIENT LIFT TRACK- MOVABLE SECONDARY RAIL.
3. PATIENT LIFT TRACK- FIXED RAIL.
4. LINE INDICATES ROOF EDGE ABOVE. CM/ROOF PLAN A42.0.
5. PRIMARY AND SECONDARY RAILS TO ALIGN TO ALLOW LIFT TRACK ASSEMBLY TO TRAVERSE BACK AND FORTH FROM BATHROOM TO GERMON ATRIUM.
6. STEEL STAIR ASSEMBLY. RE: A44.0.
7. CEILING MOUNTED-SHOWER CURTAIN TRACK ON BOTH SIDES OF SHOWER, ONE ON EACH SIDE OF FIXED PATIENT LIFT TRACK.
8. CEILING MOUNTED PATIENT PRIVACY CURTAIN. RE: A47.2-6.
9. CEILING MOUNTED PATIENT PRIVACY CURTAIN. DIVIDED BY FIXED PATIENT LIFT TRACK. PROVIDE CURTAINS FOR EACH SIDE OF PATIENT LIFT TRACK.
10. PATIENT LIFT TRACK-- HEAVY DUTY SECONDARY RAIL.
11. PATIENT LIFT TRACK-- HEAVY DUTY FIXED RAIL.
12. TWO LAYERS OF GYPSUM BOARD AT CEILING ASSEMBLY.
13. 22" x24" (0.56m x 1.52m) ACCESS HATCH
14. 24" x24" (0.61m x 0.61m) ACCESS PANEL
15. ROOF OVERFLOW PENETRATION, PROVIDE ESCUTCHEON

LEGEND:

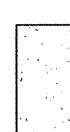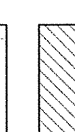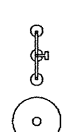
- | | |
|---|---|
|  | HATCH INDICATES 2x4 ACOUSTICAL CEILING |
|  | HATCH INDICATES SUSPENDED GYPSUM BOARD CEILING ASSEMBLY |
|  | HATCH INDICATES SUSPENDED GYPSUM BOARD CEILING ASSEMBLY WITH 2 LAYERS OF GYPSUM BOARD |
|  | LIGHT FIXTURE, CW/ELECTRICAL |
|  | MECHANICAL, CW/ MECHANICAL |
|  | LINE INDICATES SMOKE PARTITION, REF. CODE PLAN AM6.1. |
|  | LINE INDICATES WALL TO EXTEND 8' A.F.C. |

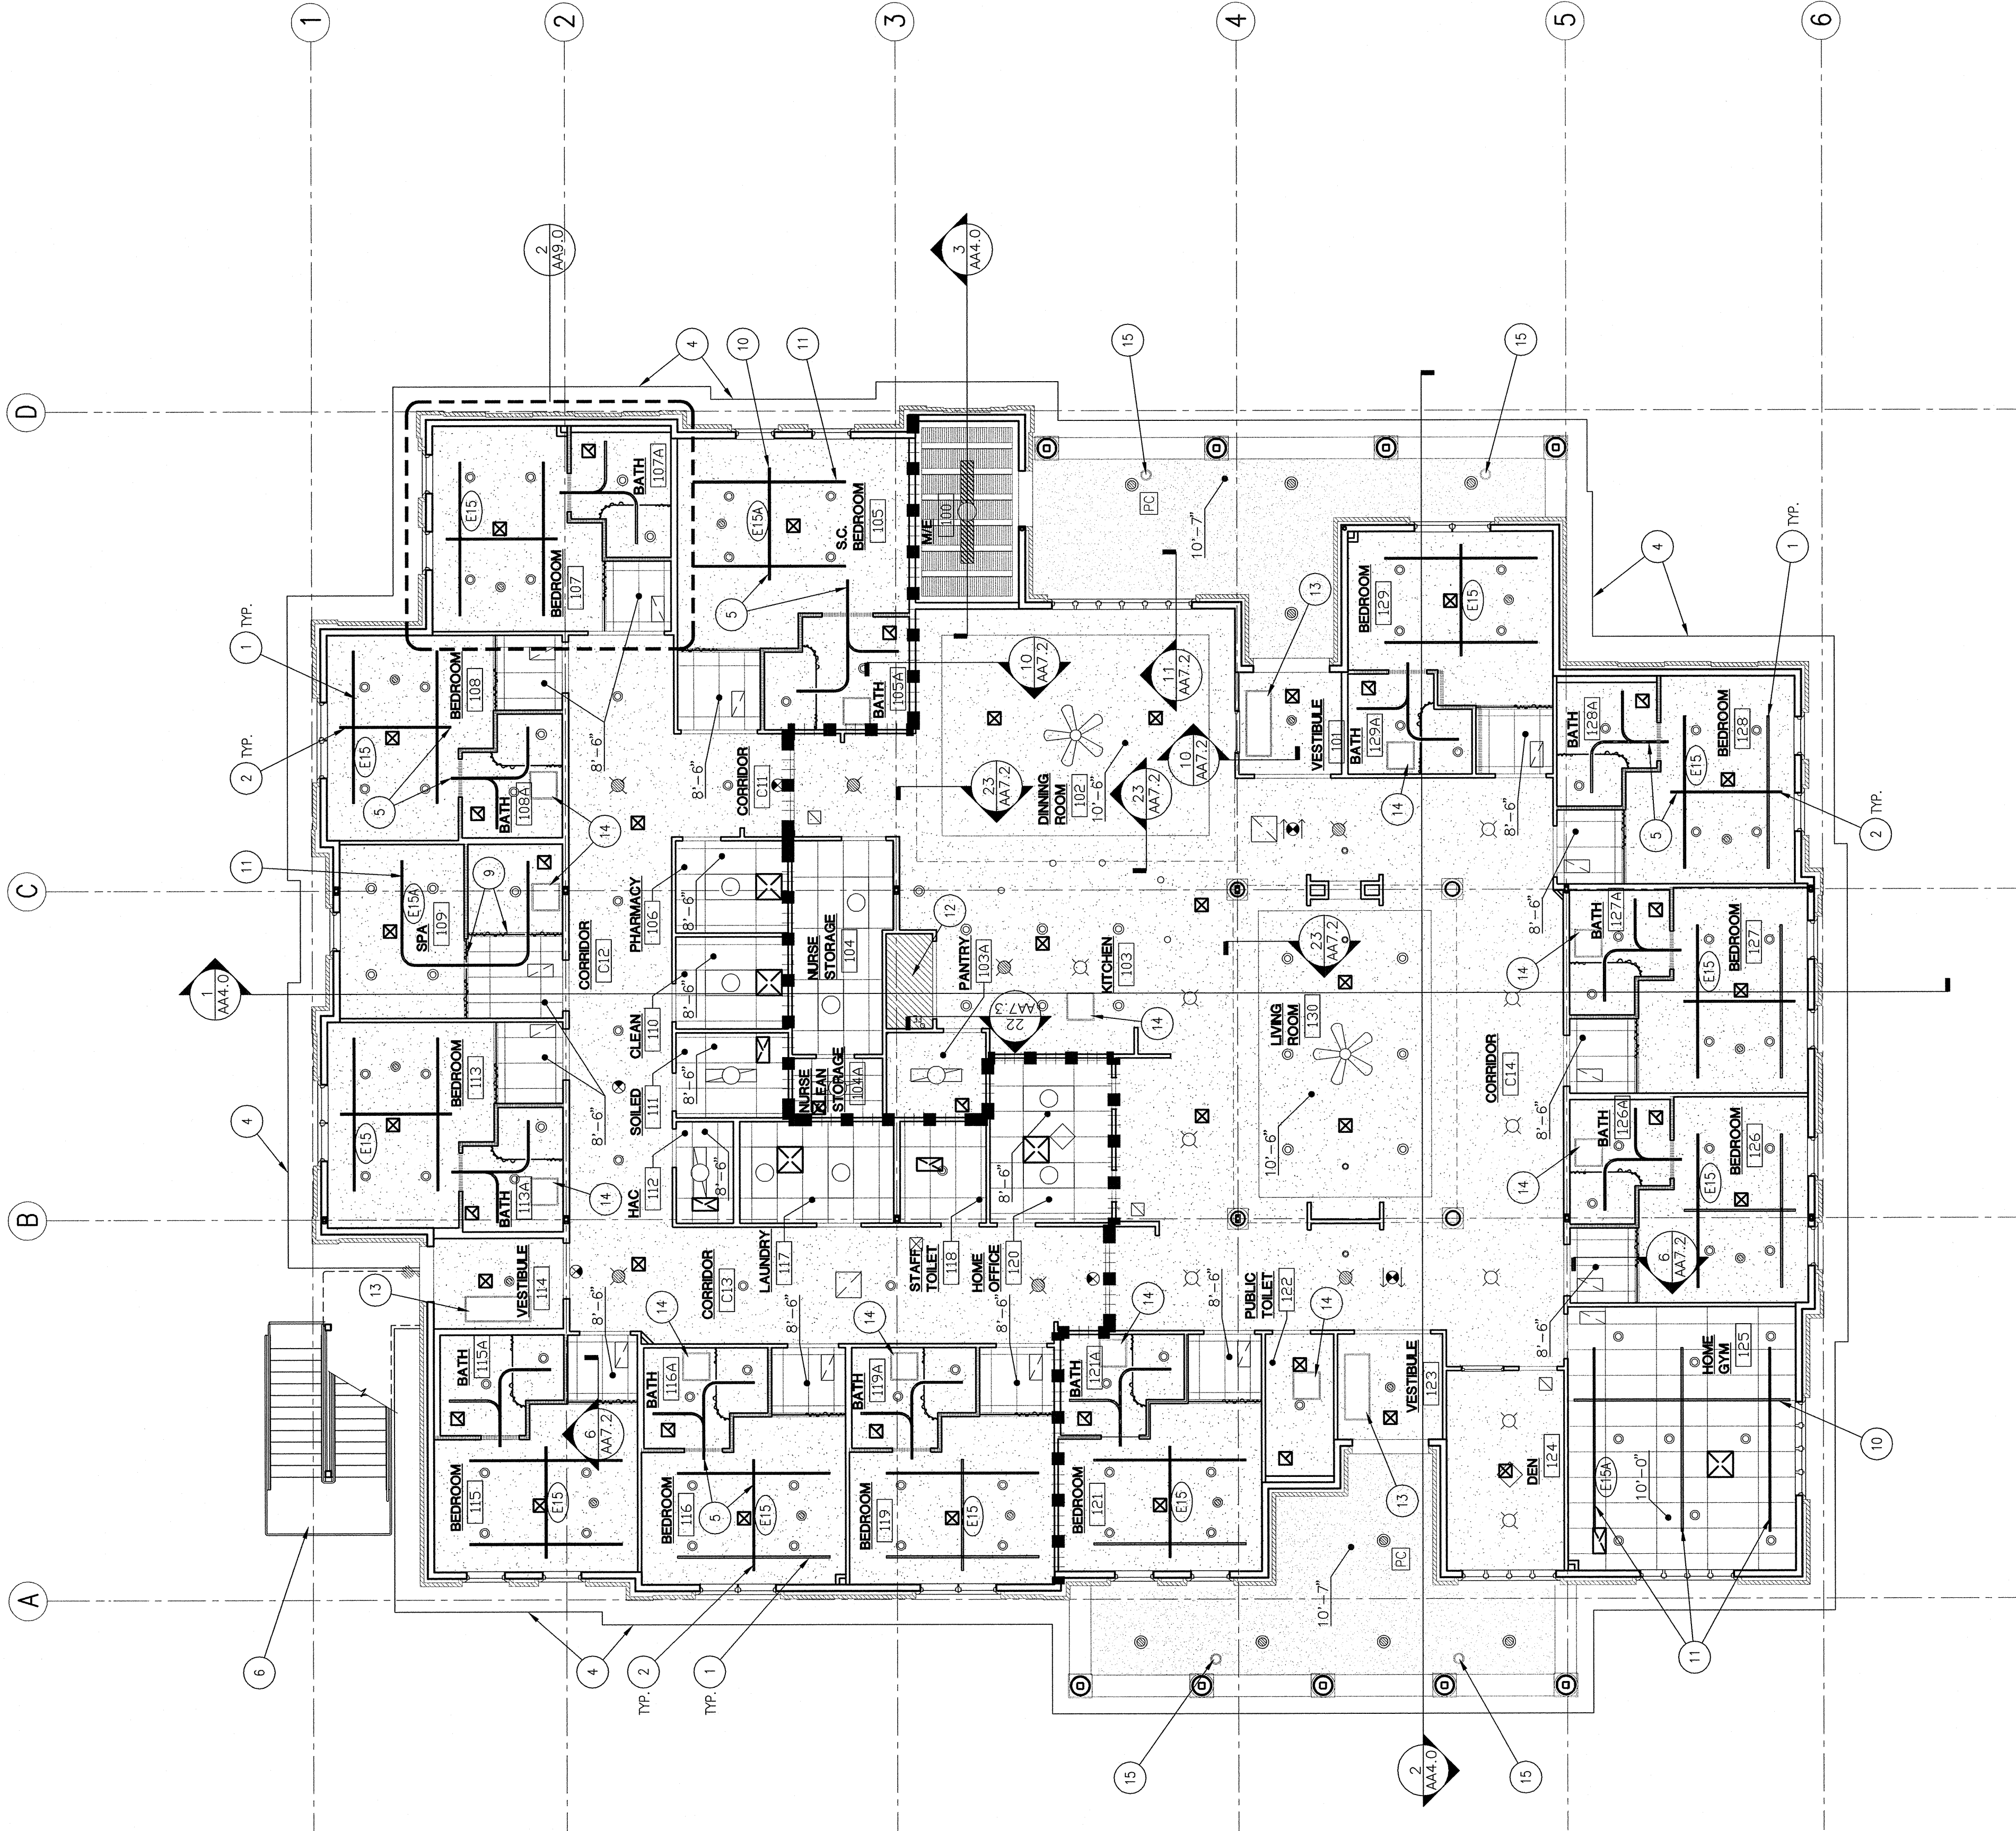


1 REFLECTED CEILING PLAN

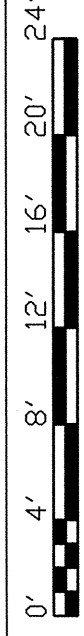


SCALE: $1/8" = 1'-0"$

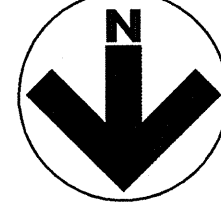

BEDROOM REFLECTED 2 CEILING PLAN, TYP.

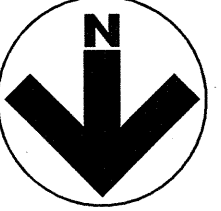

SCALE: 1/4" = 1'-0"

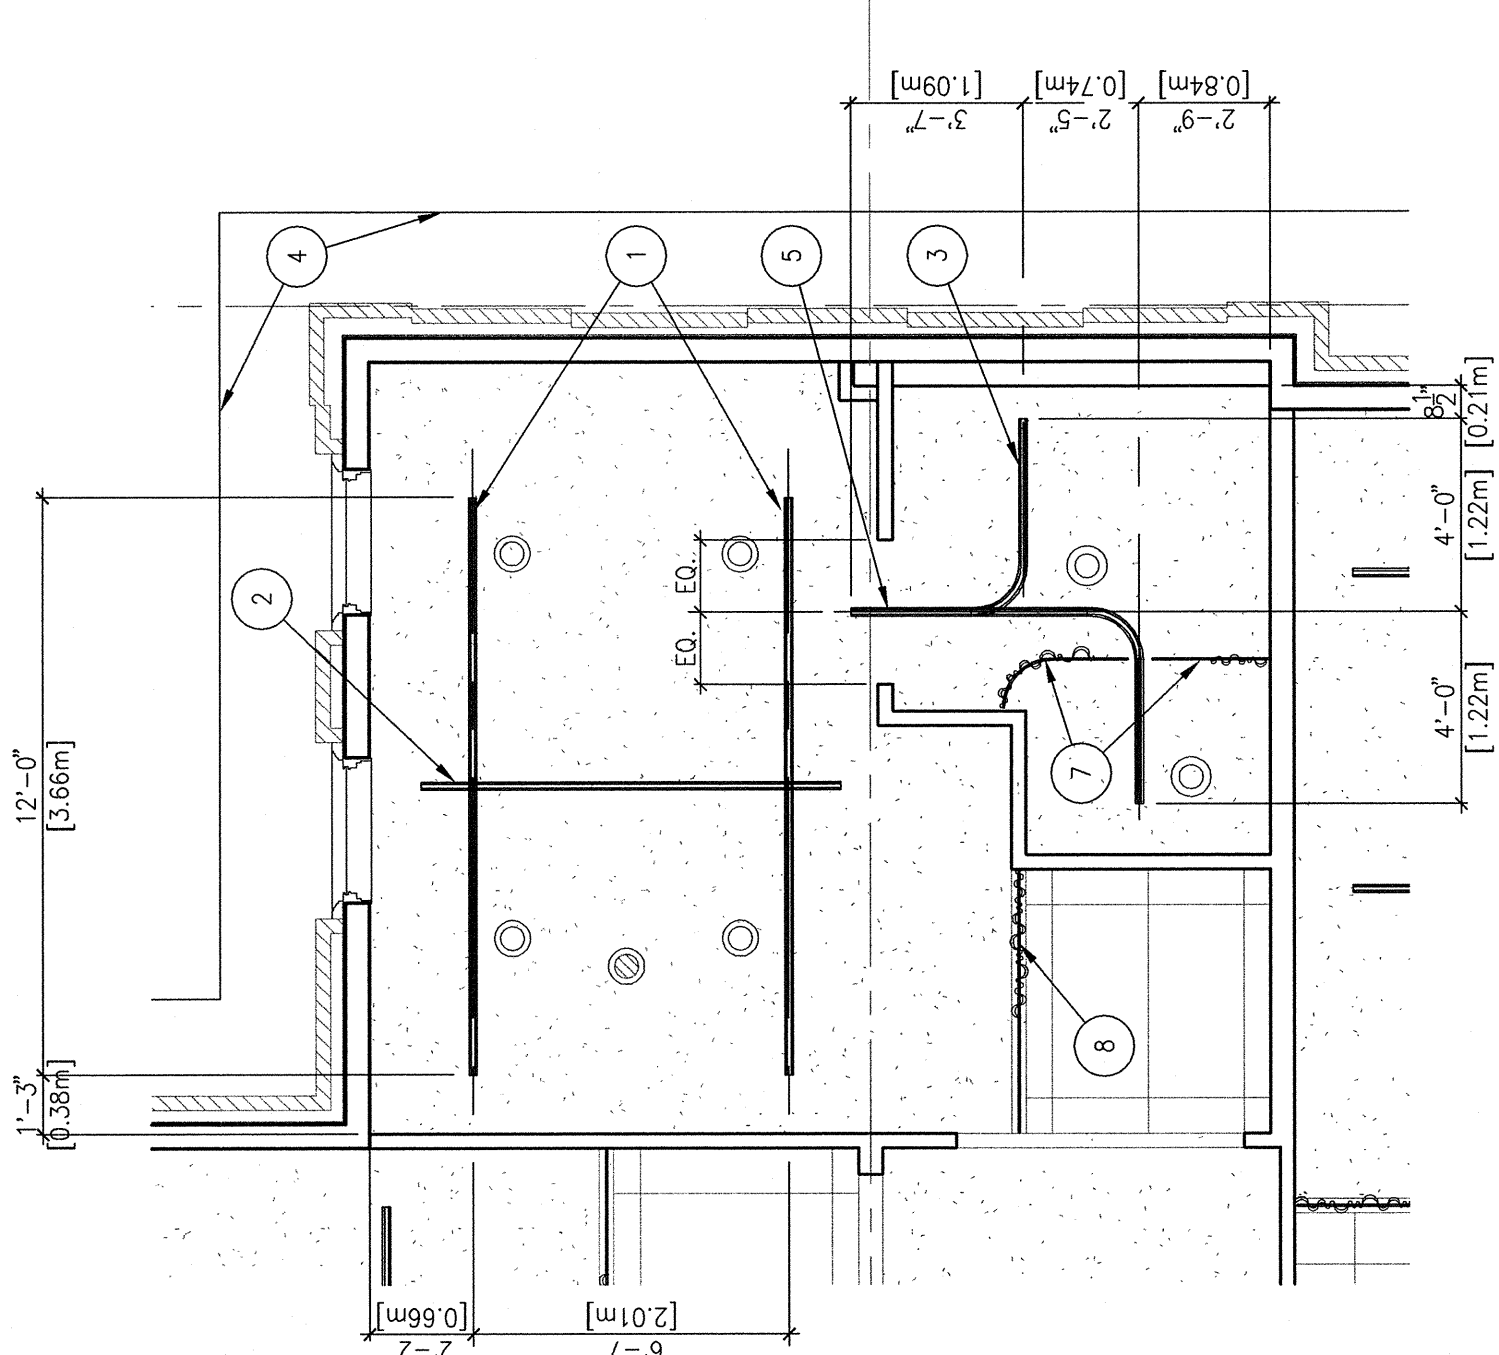

REVISIONS	DATE

CSHQ

C.W. MOORE PLAZA
250 S. 5TH ST. BOISE, ID 83702
(208) 343-4635 FAX (208) 343-1858
<http://www.cshqa.com>

JOHN D. MAULIN, ARCHITECT
C.W. MOORE PLAZA
620 S. 5TH ST.
BOISE, IDAHO
PHONE: 208-343-4635 FAX: 208-343-1658

LICENSED ARCHITECT
 AR 1708
 JOHN D. MAULIN
 STATE OF IDAHO
 ORIGINAL DOCUMENT
 SIGNED BY ARCHITECT OR
 FILE WITH THE OWNER
 ORIGINAL SIGNED BY:
 JOHN D. MAULIN
 ORIGINAL DATE SIGNED:
 DECEMBER 01, 2011

CAD FILE NAME:
531-319_AA9.0.DWG

XREF FILE NAME:
531-319_xA_30X42TLBK.DWG
531-319_xA_BASE1.DWG
531-319_xA_LIGHTING.DWG

DRAWING TITLE
REFLECTED CEILING PLANS

APPROVED: CHIEF OF FACILITY MANAGEMENT SERVICE

LOCATION VAMC BOISE IDAHO

PROJECT TITLE
BOISE VAMC
NEW EXTENDED CARE UNIT
BUILDING 'A' CLC

DRAWING NO.

C

0.000000

DATE 12/01/2011

REVISIONS