

REPAIR AND WEATHERIZE PARKING STRUCTURE 211 ELEVATOR


SAN FRANCISCO VA MEDICAL CENTER, SAN FRANCISCO - CA

PROJECT #: 662-23-111

DRAWING INDEX

PAGE #	SHEET #	SHEET NAME
--------	---------	------------

GENERAL		
1 OF 17	G-001	COVER SHEET
ARCHITECTURAL		
2 OF 17	A-001	ARCH SYMBOLS, ABBREVIATIONS, & GENERAL NOTES
3 OF 17	AD101	LEVEL 4 - ELEVATOR LOBBY - DEMOLITION PLAN
4 OF 17	AE101	LEVEL 4 - ELEVATOR LOBBY - ENLARGED PLAN
5 OF 17	AE420	EXTERIOR ELEVATIONS
6 OF 17	A-601	ELEVATOR SCOPE, DOOR SCHEDULE, TYPES & DETAILS
STRUCTURAL		
7 OF 17	S-001	STRUCTURAL GENERAL NOTES
8 OF 17	S-002	ABBREVIATIONS AND SYMBOLS
9 OF 17	S-101	LEVEL 4 - STRUCTURAL PLAN AND ELEVATIONS
PLUMBING		
10 OF 17	P-101	PLUMBING FLOOR PLANS
ELECTRICAL		
11 OF 17	E-001	ABBREVIATIONS, GENERAL NOTES, AND SHEET INDEX
12 OF 17	E-002	ELECTRICAL LEGENDS
13 OF 17	E-101	ELECTRICAL FLOOR PLAN - LEVEL 1
14 OF 17	E-104	ELECTRICAL FLOOR PLAN - LEVEL 4
15 OF 17	E-501	ELECTRICAL DETAILS
16 OF 17	E-601	ONE-LINE DIAGRAM
17 OF 17	E-701	ELECTRICAL SCHEDULES

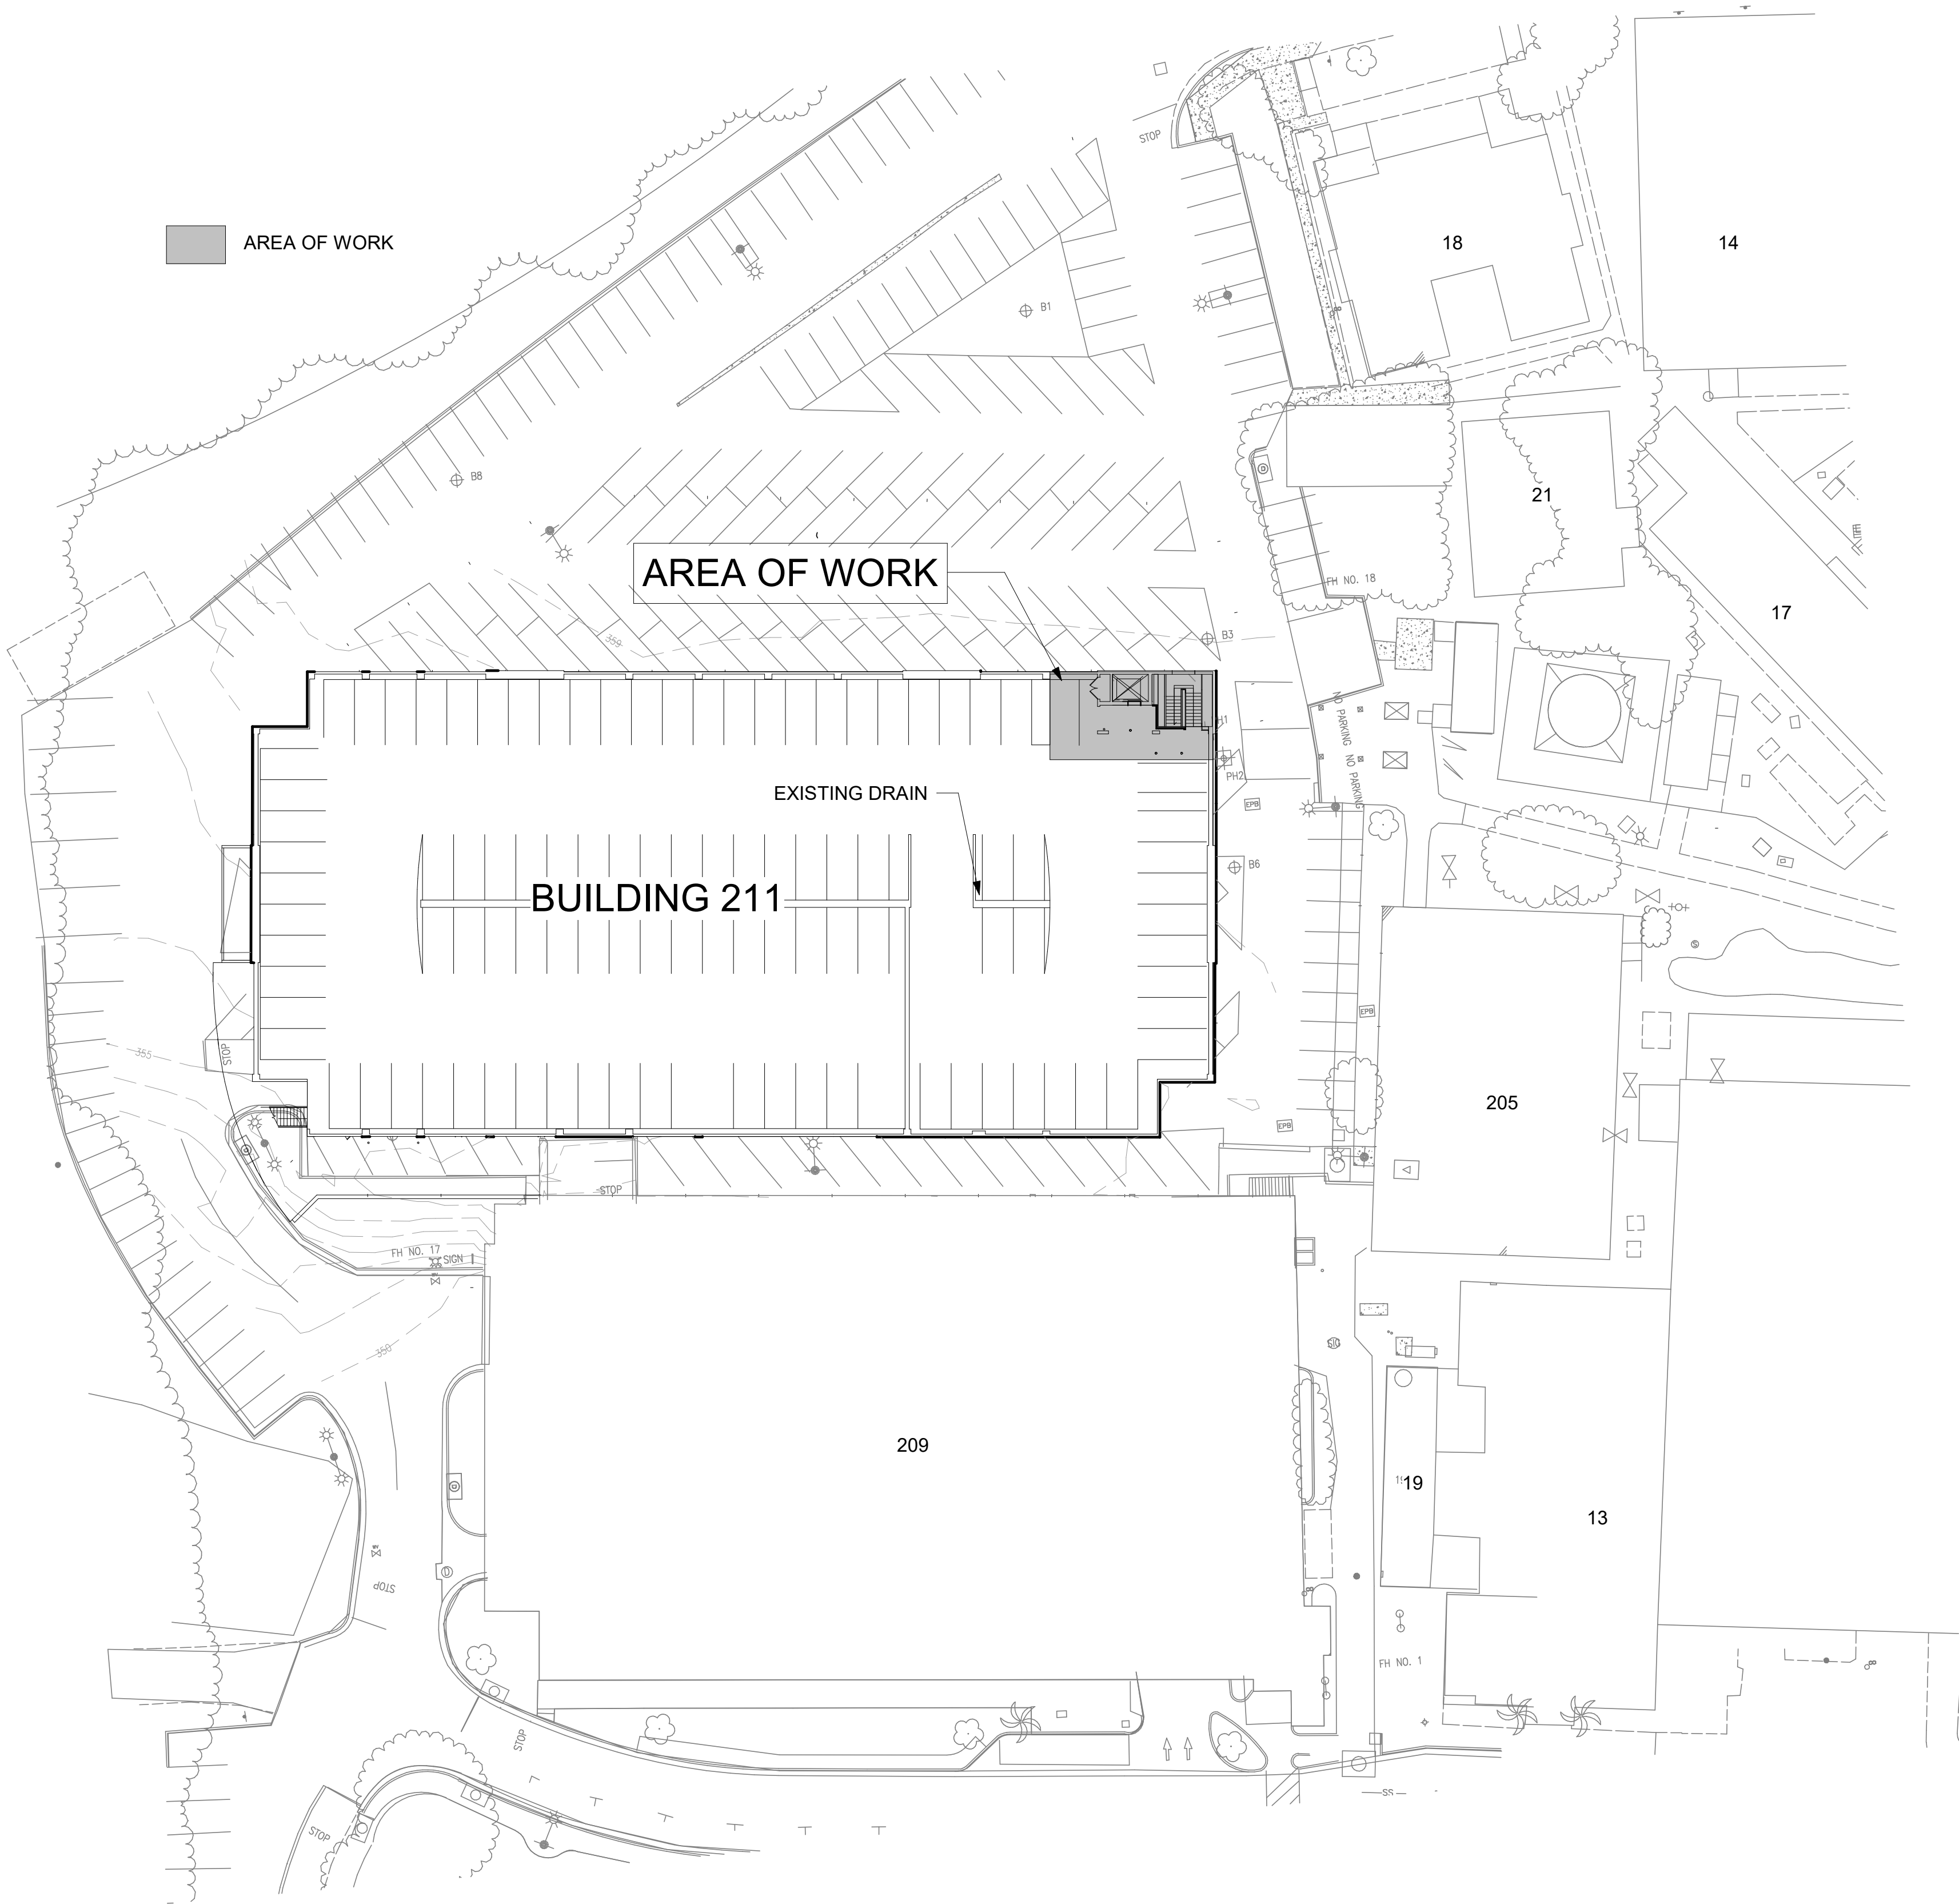

2 SITE PLAN
1" = 30'-0"



CD SET APPROVAL

DEPARTMENT OF VETERANS AFFAIRS
PROJECT #: 662-24-111

APPROVED BY: _____ DATE _____
FREDERIC CHUNG, CONTRACTING OFFICER REPRESENTATIVE

APPROVED BY: _____ DATE _____
CHAREE HARRIS, CONTRACTING OFFICER

APPROVED BY: _____ DATE _____
DAVID ROVNER, CONTRACT SPECIALIST

PROJECT INFORMATION

CODE ANALYSIS
STATE: CALIFORNIA
COUNTY: SAN FRANCISCO
JURISTICTICION: SAN FRANCISCO

OWNER: GOV, VETERANS AFFAIRS
CONST TYPE: EXISTING (NOT ALTERED)

PROJECT DESCRIPTION
REPAIR OF EXISTING ELEVATOR
COMPONENTS AND CREATION OF A
SHELTERED LOBBY ON THE FOURTH FLOOR.

APPLICABLE BUILDING & LEVEL
BUILDING 211, LEVEL 4

DESIGN TEAM

ARCHITECT

SPEES DESIGN BUILD
625 1ST AVE, STE 301
SEATTLE, WA 98104
PHONE: (206) 590-2118

MECHANICAL

SPEES DESIGN BUILD
625 1ST AVE, STE 301
SEATTLE, WA 98104
PHONE: (206) 590-2118

ELECTRICAL

SPEES DESIGN BUILD
625 1ST AVE, STE 301
SEATTLE, WA 98104
PHONE: (206) 590-2118

ELEVATOR

NORTHBAY ELEVATOR
3715 SANTA ROSA AVE
SANTA ROSA, CA 95407
PHONE: (707) 583-3100

STRUCTURAL

WSP
9177 SKY PARK COURT
SAN DIEGO, CA 92123
PHONE: (858) 500-4525

GENERAL NOTES

- DO NOT SCALE DRAWINGS.

Revisions:	Date:

CONSULTANT
ENGINEERING DISCIPLINE:

ARCHITECT/ENGINEER OF RECORD
A/E:
SPEES DESIGN BUILD
23830 PACIFIC HIGHWAY S, SUITE 300
KENT, WA 98032



Drawing Title
COVER SHEET

Approved:

Phase
100% CONSTRUCTION
DOCUMENTS

Project Title
REPAIR AND WEATHERIZE
PARKING STRUCTURE 211
ELEVATOR

Location
SAN FRANCISCO VA MEDICAL CENTER - SAN
FRANCISCO, CA

Issue Date
11/17/2025
Checked
MK
Drawn
AJ


Project Number
662-23-111
Building Number

Drawing Number
G-001


SYMBOLS			
	EXTERIOR ELEVATION		EXISTING TO REMAIN
	INTERIOR ELEVATION		NEW CONSTRUCTION
	BUILDING SECTION FLAG		TO DEMOLISH (DEMO SHEET(S) ONLY)
	WALL SECTION FLAG		ABOVE
	CALLOUT FLAG		BELOW
	VERTICAL GRID LINE		EXISTING DOOR TO REMAIN
	HORIZONTAL GRID LINE		EXISTING DOOR TO DEMOLISH (DEMO SHEET(S) ONLY)
	TRUE NORTH ARROW		NEW DOOR
	PROJECT NORTH ARROW (TRUE NORTH DASHED)		AREA SHOWN ON SHEET
	ELEVATION / LEVEL MARKER		OUT OF SCOPE
	KEY NOTE		INACCESSIBLE DURING PHASE (ICRA SHEET(S) ONLY)
	ROOM TAG (SF OPTIONAL)		TEMPORARY ICRA BOUNDRY (ICRA SHEET(S) ONLY)
	CEILING HEIGHT TAG		TEMPORARY ICRA BARRIER (ICRA SHEET(S) ONLY)
	WALL TAG		TEMPORARY ICRA DOOR (ICRA SHEET(S) ONLY)
	FLOOR TAG		ADHESIVE WALK-OFF MATS (ICRA SHEET(S) ONLY)
	ROOF TAG		TEMPORARY ICRA AIR PRESSURE (ICRA SHEET(S) ONLY)
	DOOR TAG		CONTRACTOR PATH OF TRAVEL (ICRA SHEET(S) ONLY)
	WINDOW TAG		SMOKE COMPARTMENT PERIMETER (FIRE LIFE SAFETY SHEET(S) ONLY)
	SPECIALTY EQUIPMENT TAG		SMOKE RATED WALL
	SIGNAGE TAG		1 HR FIRE RATED WALL
	SIGNAGE KEY NOTE (AW SHEETS ONLY)		2 HR FIRE RATED WALL
	SIGNAGE MATERIAL TAG (AW SHEETS ONLY)		SMOKE & 1 HR FIRE RATED WALL
			FIRE EXTINGUISHER CABINET (FIRE LIFE SAFETY SHEET(S) ONLY)
			EMERGENCY EGRESS ROUTE (FIRE LIFE SAFETY SHEET(S) ONLY)
			SPRINKLER PER FIRE PROTECTION
			DIFFUSER PER MECHANICAL (SIZE & PROPORTION MAY VARY)
			LIGHT FIXTURE PER ELECTRICAL (SIZE & PROPORTION MAY VARY)
MATERIALS			
	EARTH		GYPSUM BOARD, TYPE 'X'
	SAND		GYPSUM BOARD, LEAD LINED
	BATT INSULATION		ACOUSTICAL CEILING TILE, 2' x 2'
	RIGID INSULATION		ACOUSTICAL CEILING TILE, 2' x 4'
	CONCRETE		
	STEEL		
	PLYWOOD, FIRE RATED		



ABBREVIATIONS			
& AND ^ ANGLE AT @ CENTERLINE DEGREES ° NUMBER #	S SYMBOLS AB ANCHOR BOLT ABA ARCHITECTURAL BARRIERS ACT A(C)T ACOUSTICAL (CEILING) TILE ACM ASBESTOS CONTAINING MATERIAL ACW ACOUSTICAL WALL ADA AMERICANS W/ DISABILITIES ACT ADJ ADJACENT A/E ARCHITECT/ENGINEER AFF ACCESS FLOOR AFF ABOVE FINISH FLOOR AGG AGGREGATE ALT ALTERNATE ALUM ALUMINUM APPROX APPROXIMATELY ARCH ARCHITECT(URAL) ASPH ASPHALT A/V AUDIO / VIDEO BARR BARRIER BATH BATHROOM BB BACKER BOARD BLD(G) BUILDING BLK(G) BLOCK(ING) BLW BELOW BM BEAM BMT(U) BONE MARROW TRANSPLANT (UNIT) BO BOTTOM OF BOC BOTTOM OF CURB BOS BOTTOM OF SLAB BRC BRACE, BRACING BRKT BRACKET BRNG BEARING BTM BOTTOM BTWN BETWEEN CAB CABINET CC CONTRACTOR FURN, CONTRACTOR INST CD CONSTRUCTION / CONTRACT DOCUMENTS CJ CONTROL JOINT CLG CEILING CLR CLEAR(ANCE) CMU CONCRETE MASONRY UNIT CO CONTRACTING OFFICER COL COLUMN COMP COMPOSITION CONC CONCRETE CONN CONNECTION CONST CONSTRUCTION CONT CONTINUOUS COORD COORDINATE COR CONTRACTING OFFICER REPRESENTATIVE CORR CORRIDOR CS CONCRETE SEALER CT CERAMIC TILE CTR CENTER CV CONTRACTOR FURNISHED, VA INSTALLED DB DESIGN BUILD DBL DOUBLE DC DIRECT CURRENT DD DESIGN DEVELOPMENT DEMO DEMOLISH(ION) DEPT DEPARTMENT DG DESIGN GUIDE DIA DIAMETER DIM DIMENSION DM DESIGN MANUAL DWN DOWN DR DOOR DTL DETAIL DWG DRAWING(S) E EAST EA EACH EJ EXPANSION JOINT ELEC ELECTRIC(AL) ELEV ELEVATION OR ELEVATOR ENG ENGINEER(ING) EOP EDGE OF CURB EOP EDGE OF PAVEMENT EPDM ETHYLENE PROPYLENE DIENE TERPOLYMER EQ EQUAL EQUIP EQUIPMENT ES EACH SIDE ETS EXPOSED TO STRUCTURE EX(IST) EXISTING EXP EXPANSION EXT EXTERIOR FA FIRE ALARM FD FLOOR DRAIN FE(C) FIRE EXTINGUISHER (CABINET) FF FACTORY FINISH FFB FINISH FLOOR BREAK FIN FINISH(ED) FLASH FLASHING FLR FLOOR(ING) FLRSNT FLORESCENT FNDN FOUNDATION FOC FACE OF CONCRETE FOF FACE OF FINISH FOS FACE OF STUDS FP FIRE PROOF FR FIRE RATED FRM FRAME FT FOOT, FEET FTG FOOTING FUR FURRING FURN FURNISHED F FIRE ALARM FLOOR DRAIN FIRE EXTINGUISHER (CABINET) FACTORY FINISH FINISH FLOOR BREAK FINISH(ED) FLASHING FLOOR(ING) FLORESCENT FOUNDATION FACE OF CONCRETE FACE OF FINISH FACE OF STUDS FIRE PROOF FIRE RATED FRAME FOOT, FEET FOOTING FURRING FURNISHED G GAGE, GAUGE GALV GALVANIZED GE GENERAL ELECTRIC G(W)B GYPSUM (WALL) BOARD GC GENERAL CONTRACTOR GL GRID LINE GLB GLUE LAMINATED BEAM GMU GLASS MASONRY UNIT GOV(T) GOVERNMENT GYP GYPSUM BOARD H HOUSEKEEPING AIDES CLOSET HEADER H(D)W(E) HARDWARE HM HOLLOW METAL HORZ HORIZONTAL HPDL HIGH PRESSURE DECORATIVE LAM HR HOUR HT HEIGHT HVAC HEATING, VENTILATION & AIR CONDITIONING I INFECTIOUS CONTROL RISK ASSESSMENT ID INSIDE DIAMETER OR DIM ILSM INTERIM LIFE SAFETY MEASURES INCL INCLUDE(D,ING) INST INSTALL INSUL INSULATION INT INTERIOR J JOINT K KILOVOLT L LAMINATE(D) LAV LAVATORY LCM LEAD CONTAINING MATERIAL(S) LD LEAD LT LIGHT M MATERIAL(S) MAX MAXIMUM MDF MEDIUM-DENSITY FIBREBOARD MECH MECHANICAL(AL) MEP MECHANICAL, ELECTRICAL, PLUMBING MFR MANUFACTURE(R) MIN MINIMUM MISC MISCELLANEOUS MOD MODIFIED MTL METAL N NORTH N(I)A NOT APPLICABLE NEG NEGATIVE NO, NUMBER NOM NOMINAL NTS NOT TO SCALE O.C. ON CENTER(S) OPN(G) OPEN(ING) OPP OPPOSITE OPT OPTION(AL) OVHD OVERHEAD P PAINT PCONC PRECAST CONCRETE PCRA PRE-CONSTRUCTION RISK ASSESSMENT PL PLATE PLAM PLASTIC LAMINATE PLY(WD) PLYWOOD PNL PANEL PR PAIR PRFB PREFABRICATED PS PLASTIC PT PORCELAIN TILE PTN(S) PARTITION(S) PVMT PAVEMENT Q QUANTITY R RADIUS RB RESILIENT BASE RCP(S) REFLECTED CEILING PLAN(S) REF REFERENCE REINF REINFORCE(D,ING) REP REPRESENTATIVE REQ(S,(Y)D) REQUIRE(D,S,MENT(S)) RESIL RESILIENT REV REVERSE RF ROOF RM ROOM RMV REMOVE RO ROUGH OPENING S SOUTH SCHED SCHEDULE SCI(D) SPINAL CORD INJURY (& DISABILITY) SD SCHEMATIC DESIGN SDSF SOLID SURFACE SECT SECTION SF SQUARE FEET SFRM SPRAY APPLIED FIRE-RESISTIVE MATERIAL SHG SHINGLES SHLD(G) SHEILD(ING) SHT(G) SHEET (SHEATHING) SIM SIMILAR SM SEAM SOW SCOPE OF WORK SPEC SPECIFICATION SQ SQUARE SS STAINLESS STEEL ST STAIN STDG STANDING STF STAFF STL STEEL STOR STORAGE STRUCT STRUCTURAL SURG SURGERY, SURGICAL SUSP SUSPENDED SV SHEET VINYL SYS SYSTEM TBD TO BE DETERMINED TBL TABLE TEMP TEMPORARY T&G TONGUE AND GROOVE THK THICK(NESS) THRESH THRESHOLD TOC TABLE OF CONTENTS TOS TOP OF SLAB TPH TOILET PAPER HOLDER TRANS TRANSITION TS TUBE STEEL TYP TYPICAL U UNLESS NOTED OTHERWISE UNLESS OTHERWISE NOTED V VETERANS AFFAIRS VAR VARIES VB VAPOR BARRIER VC VA FURNISHED, CONTRACTOR INSTALLED VERT VERTICAL VIF VERIFY IN FIELD VV VA FURNISHED, VA INSTALLED W WEST W/ WITH WD WOOD WDW WINDOW WGHT WEIGHT W/O WITHOUT WP WATERPROOF(ING) WR WATER RESISTANT WRK WORK X X-RAY Y Y Z Z AA AA BB BB CC CC DD DD EE EE FF FF GG GG HH HH II II JJ JJ KK KK LL LL MM MM NN NN OO OO PP PP QQ QQ RR RR SS SS TT TT UU UU VV VV WW WW XX XX YY YY ZZ ZZ		

Revisions: Date:		CONSULTANT		ARCHITECT/ENGINEER OF RECORD		STAMP	Office of Capital Projects		Drawing Title		Phase		Project Title		Project Number				
		ENGINEERING DISCIPLINE:		SPEES DESIGN BUILD 23830 PACIFIC HIGHWAY S, SUITE 300 KENT, WA 98032					ARCH SYMBOLS, ABBREVIATIONS, & GENERAL NOTES		100% CONSTRUCTION DOCUMENTS		REPAIR AND WEATHERIZE PARKING STRUCTURE 211 ELEVATOR		662-23-111				
									Approved:				Location SAN FRANCISCO VA MEDICAL CENTER - SAN FRANCISCO, CA		Building Number				
													Issue Date 11/17/2025		Drawing Number				
													Checked MK		Drawn AJ				
						11/12/2025	U.S. Department of Veterans Affairs								A-001				

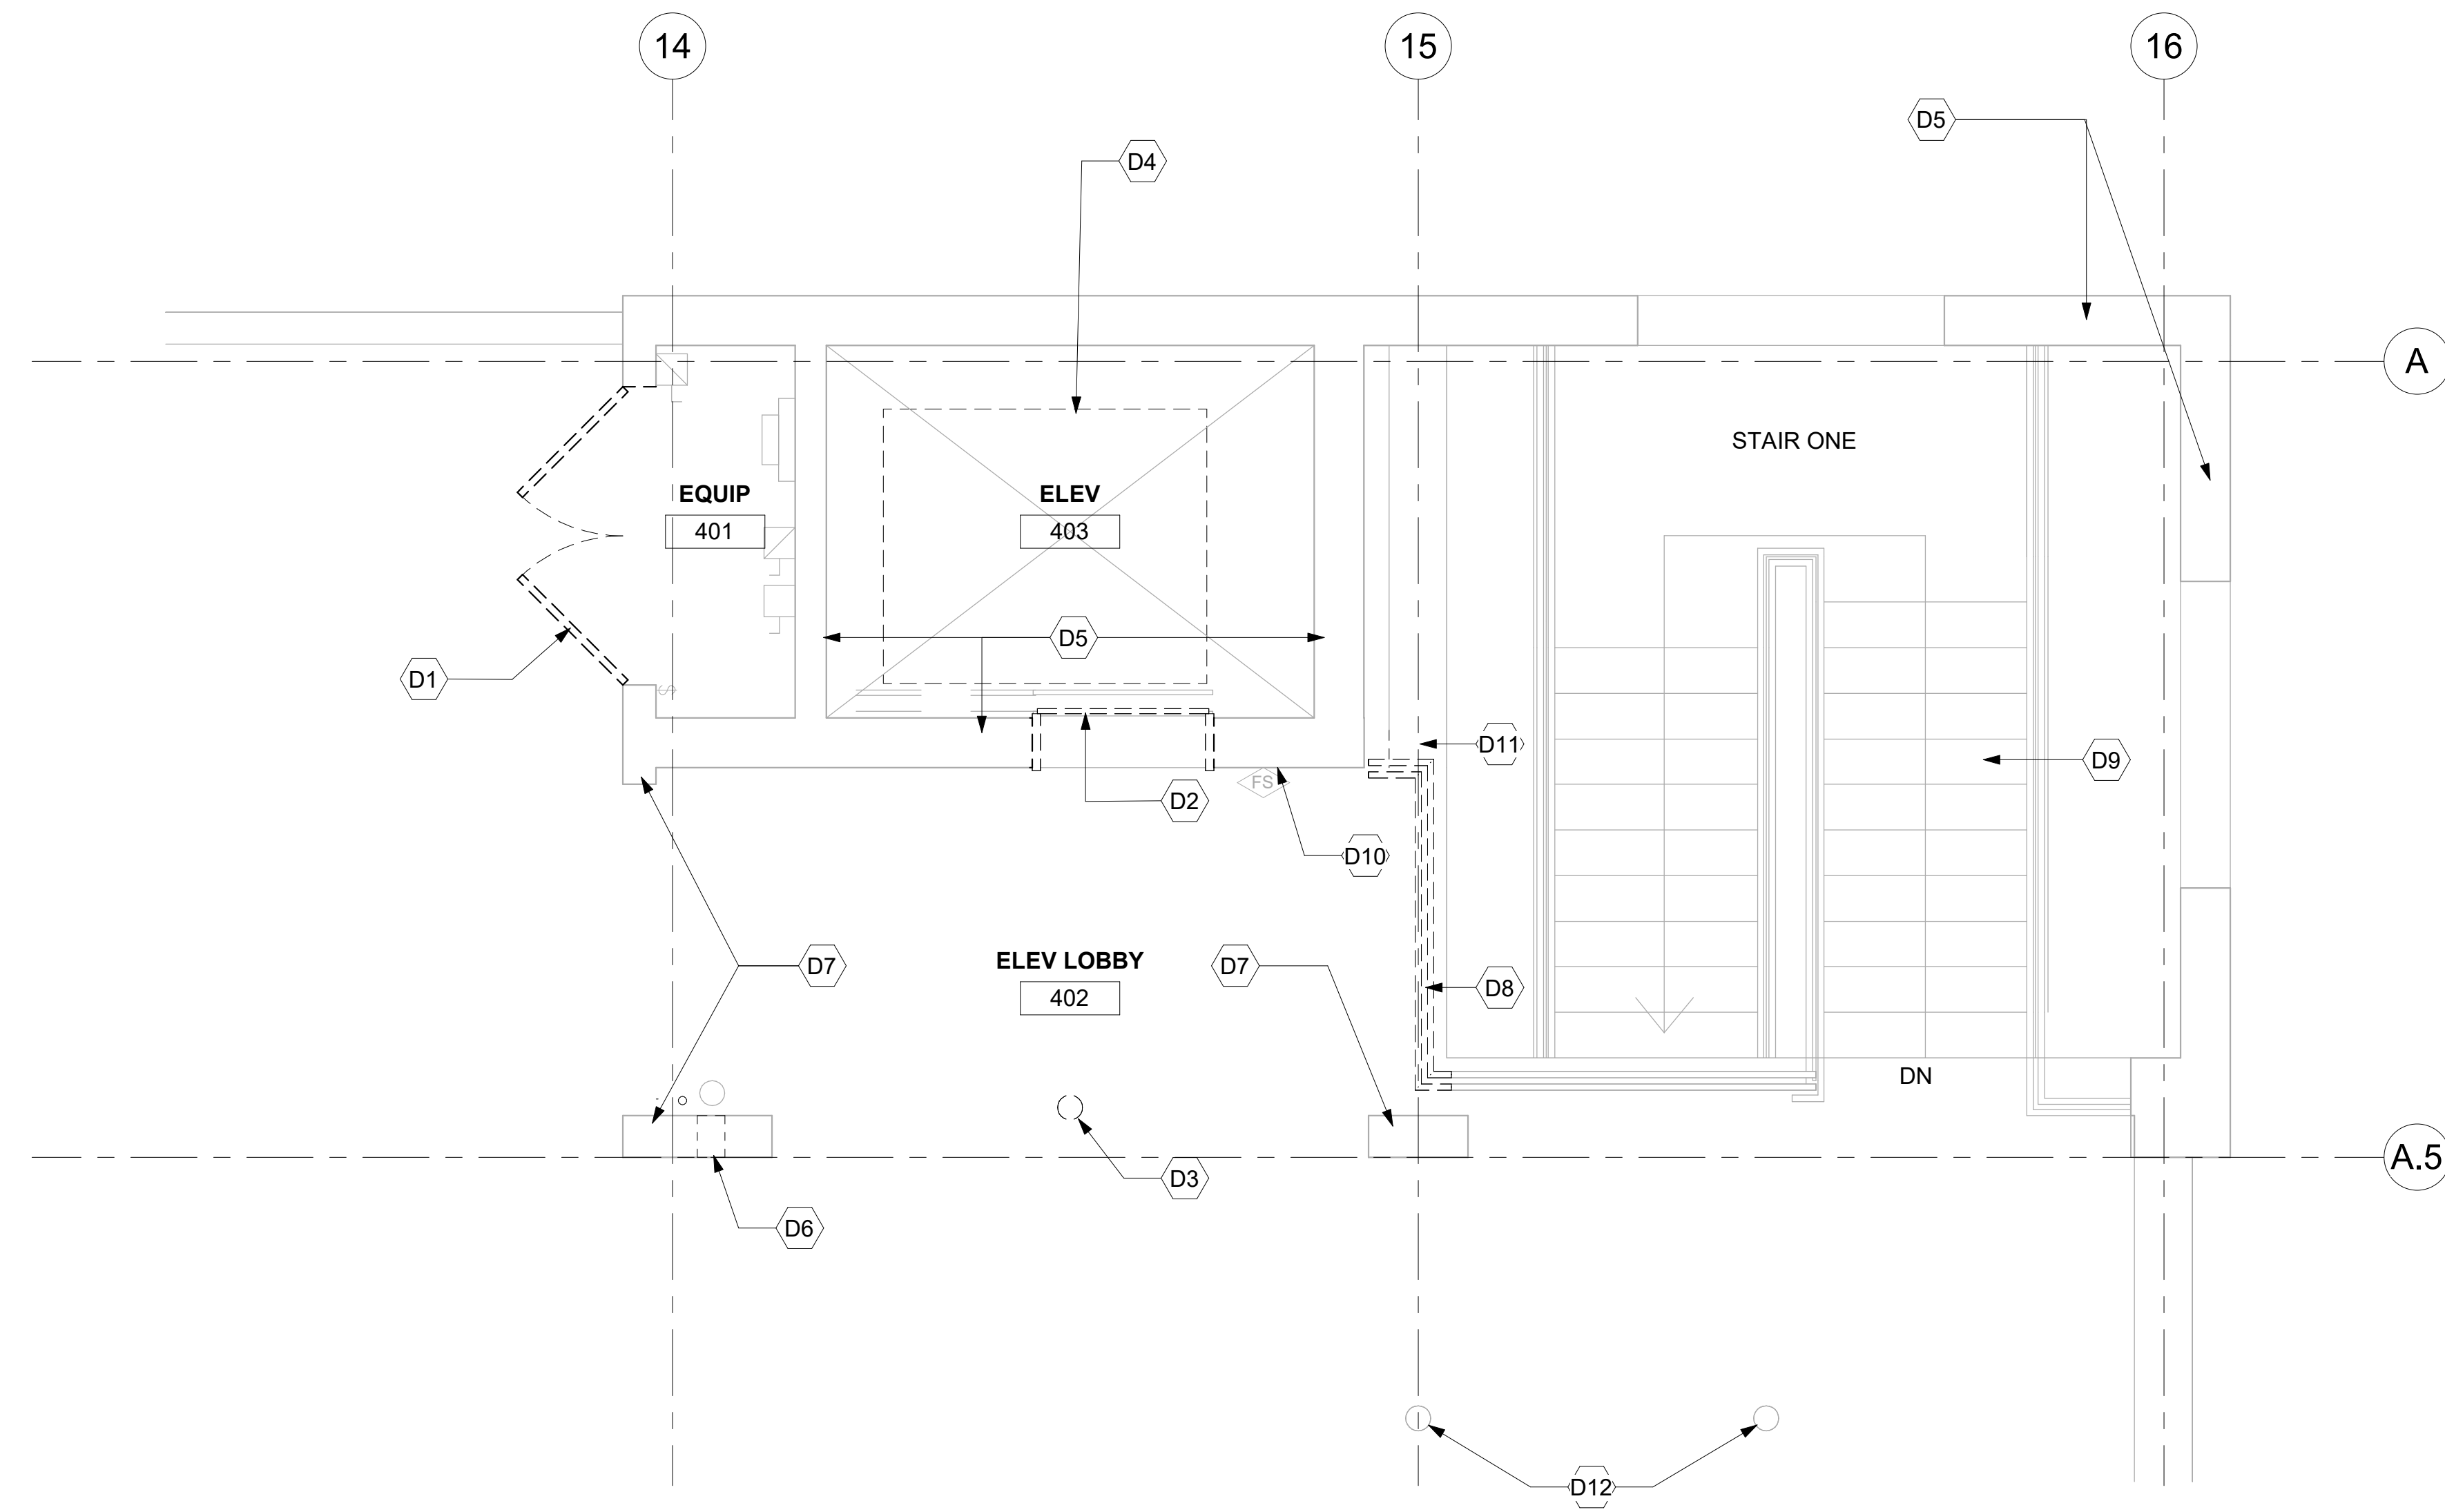

1 LEVEL 4 - ENLARGED ELEVATOR LOBBY - DEMOLITION PLAN
3/8" = 1'-0"

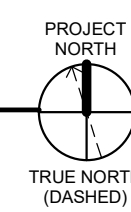


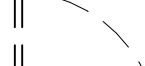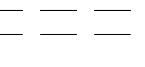
LEGEND	
	EXISTING DOOR TO REMAIN
	EXISTING DOOR TO DEMOLISH
	TO DEMOLISH
	EXISTING TO REMAIN
# KEY NOTES (THIS SHEET ONLY)	
D1	DEMOLISH EXISTING DOOR AND FRAME.
D2	DEMOLISH EXISTING ELEVATOR DOOR. EXISTING JAMB TO REMAIN.
D3	REMOVE EXISTING BOLLARD. SALVAGE FOR RELOCATION.
D4	DEMOLISH EXISTING ELEVATOR ON SCOPE OF WORK, SEE SHEET A-601.
D5	EXISTING CMU WALLS, NO WORK.
D6	DRILL EXISTING CONCRETE WALL FOR DRAIN PENETRATION.
D7	EXISTING CONCRETE WALLS, PREP FOR NEW STOREFRONT SYSTEM.
D8	DEMO EXISTING RAILING AS NEEDED FOR NEW WORK. MAXIMUM GAP BETWEEN GUARDRAIL AND GLAZING NOT TO EXCEED 3.5".
D9	EXISTING STAIRWAY, NO WORK.
D10	EXISTING STROBE/PULL STATION TO REMAIN.
D11	DEMO EXISTING SHEET METAL COVER AS NEEDED FOR NEW STOREFRONT.
D12	EXISTING BOLLARD TO REMAIN.

GENERAL NOTES


1. REMOVE WALL MOUNTED ACCESSORIES REQUIRED TO COMPLETE A CONSTRUCTION TASK. VERIFY WITH COR BEFORE DISPOSAL.
2. COORDINATE WITH VA COR PRIOR TO THE DEMOLITION OF ANY EXISTING EQUIPMENT.

KEY PLAN

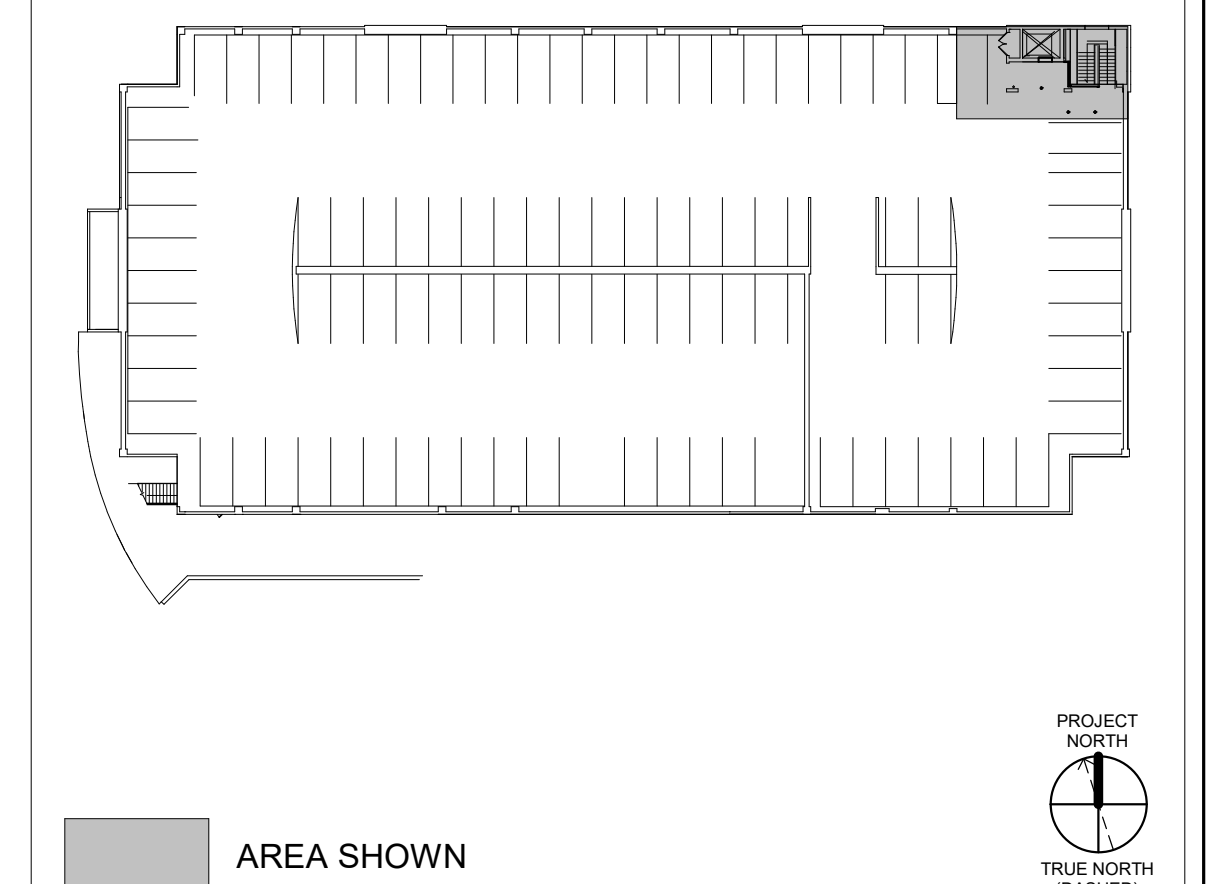[illegible]

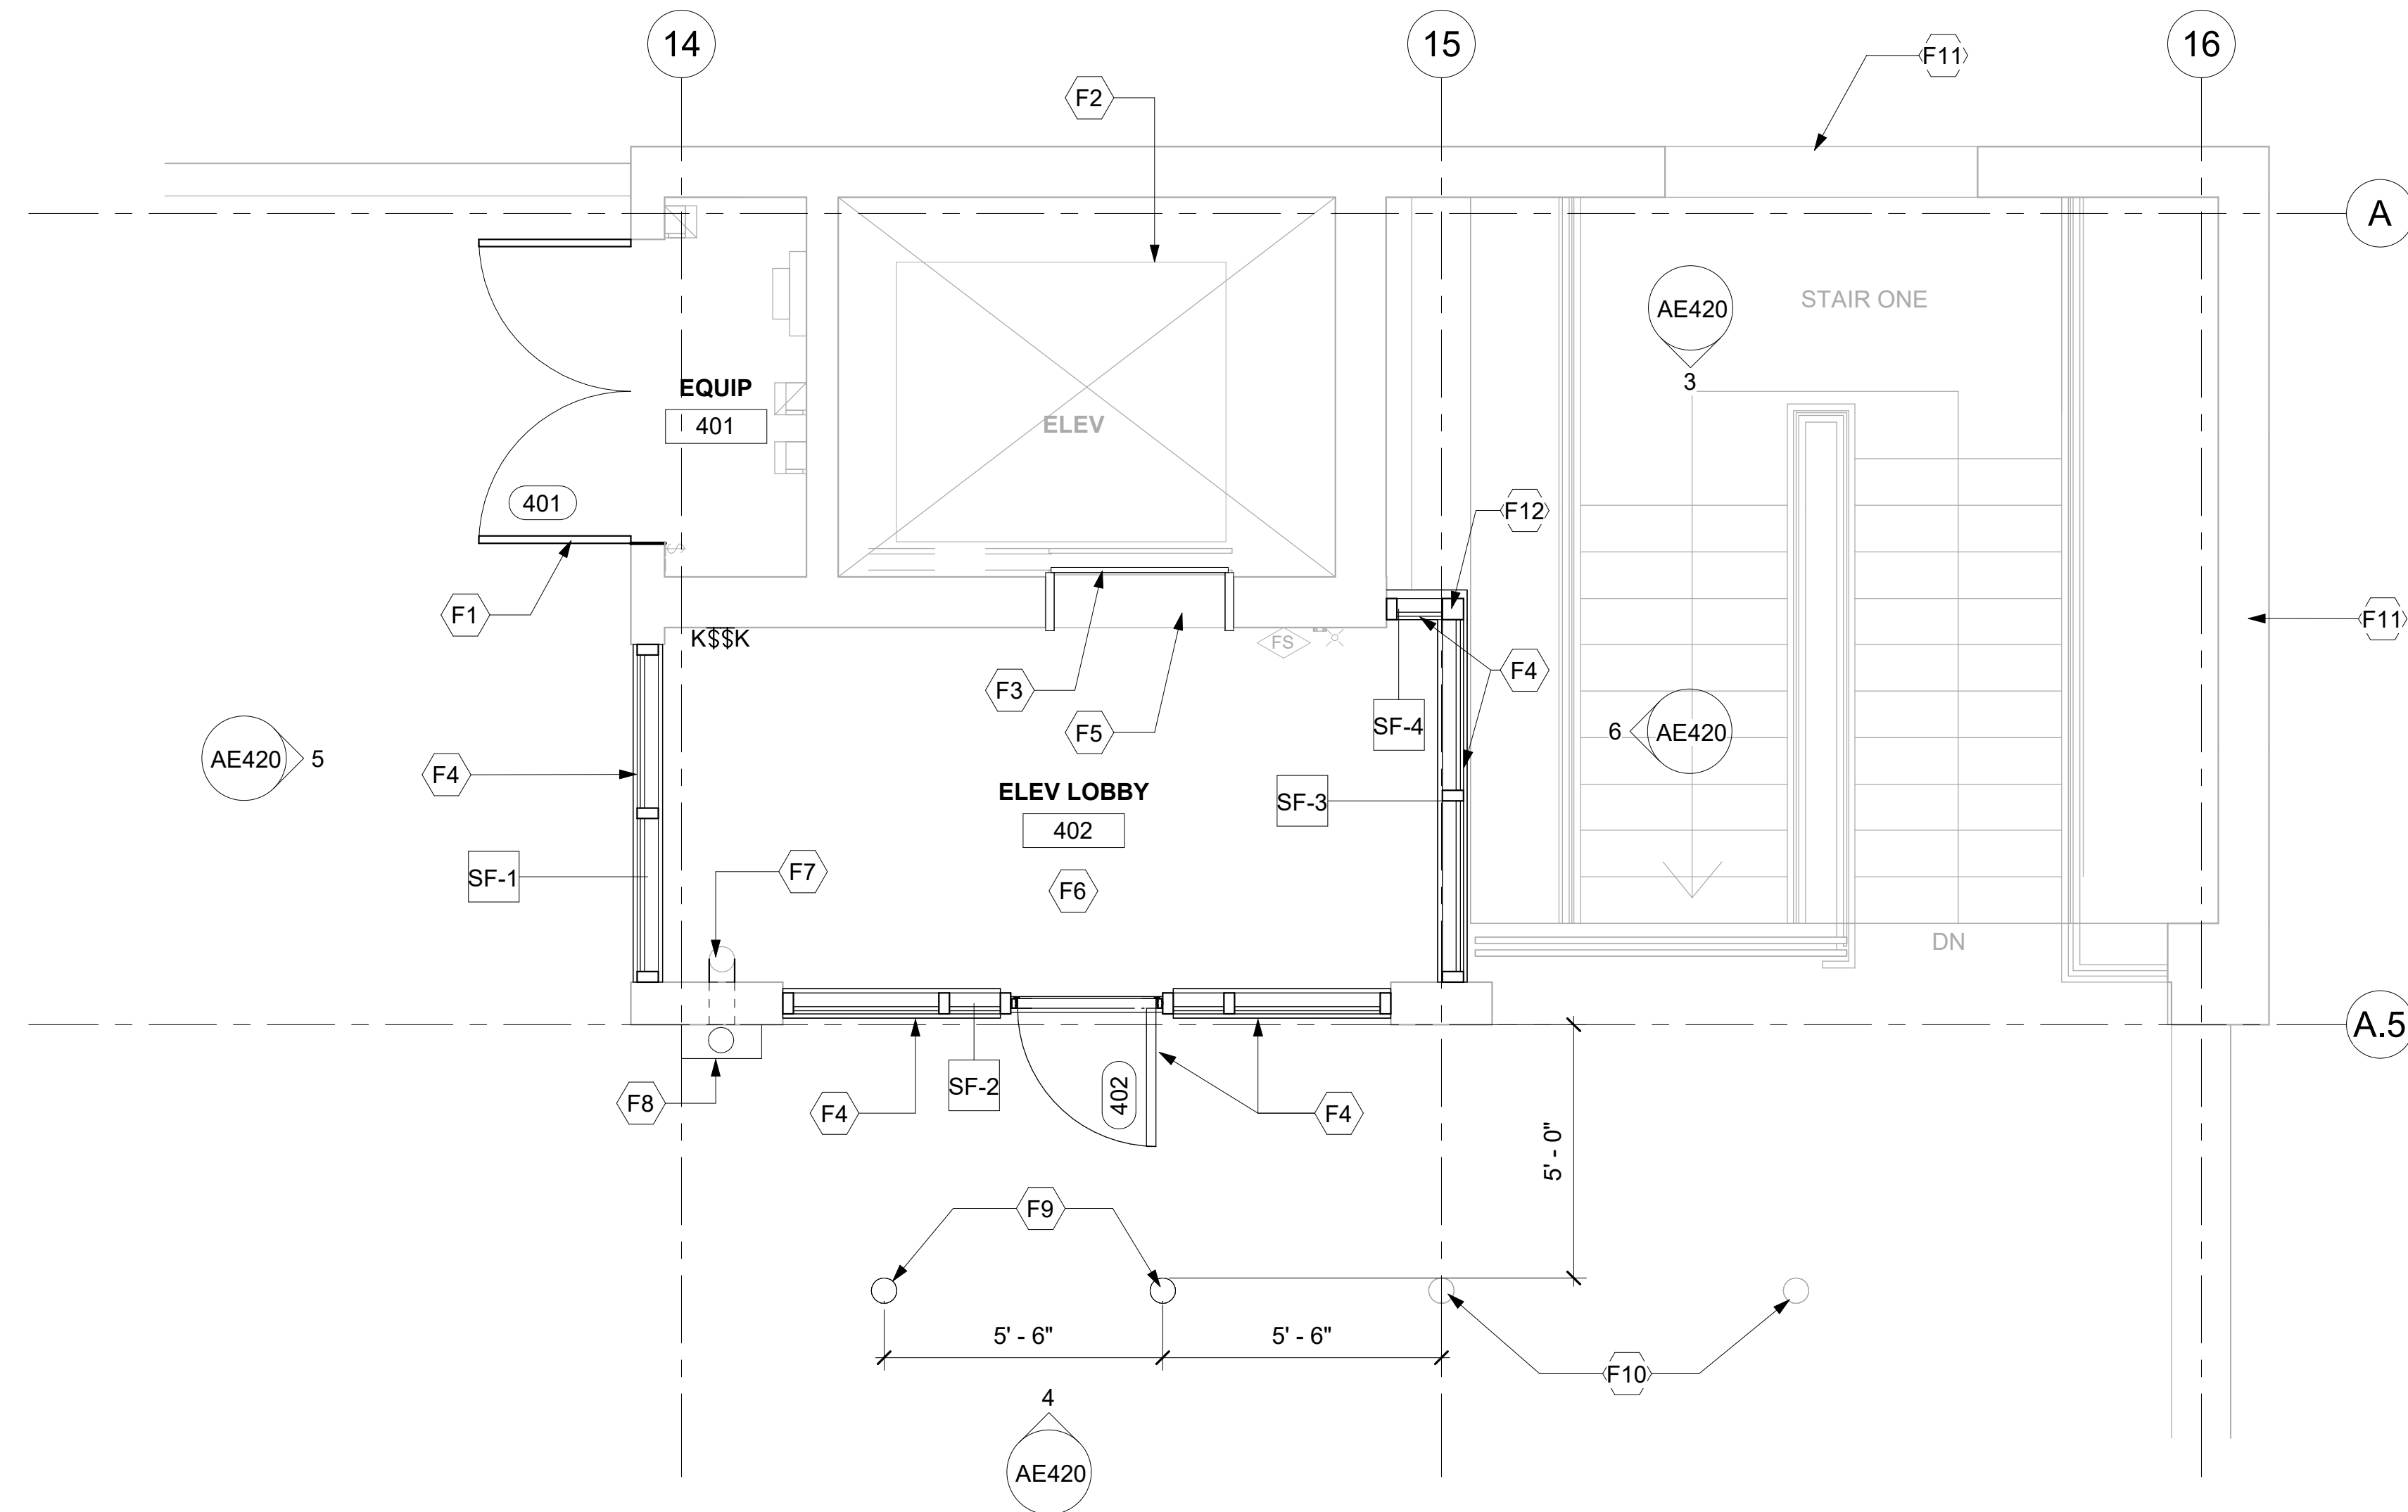


1 LEVEL 4 - ELEVATOR LOBBY - ENLARGED PLAN
3/8" = 1'-0"

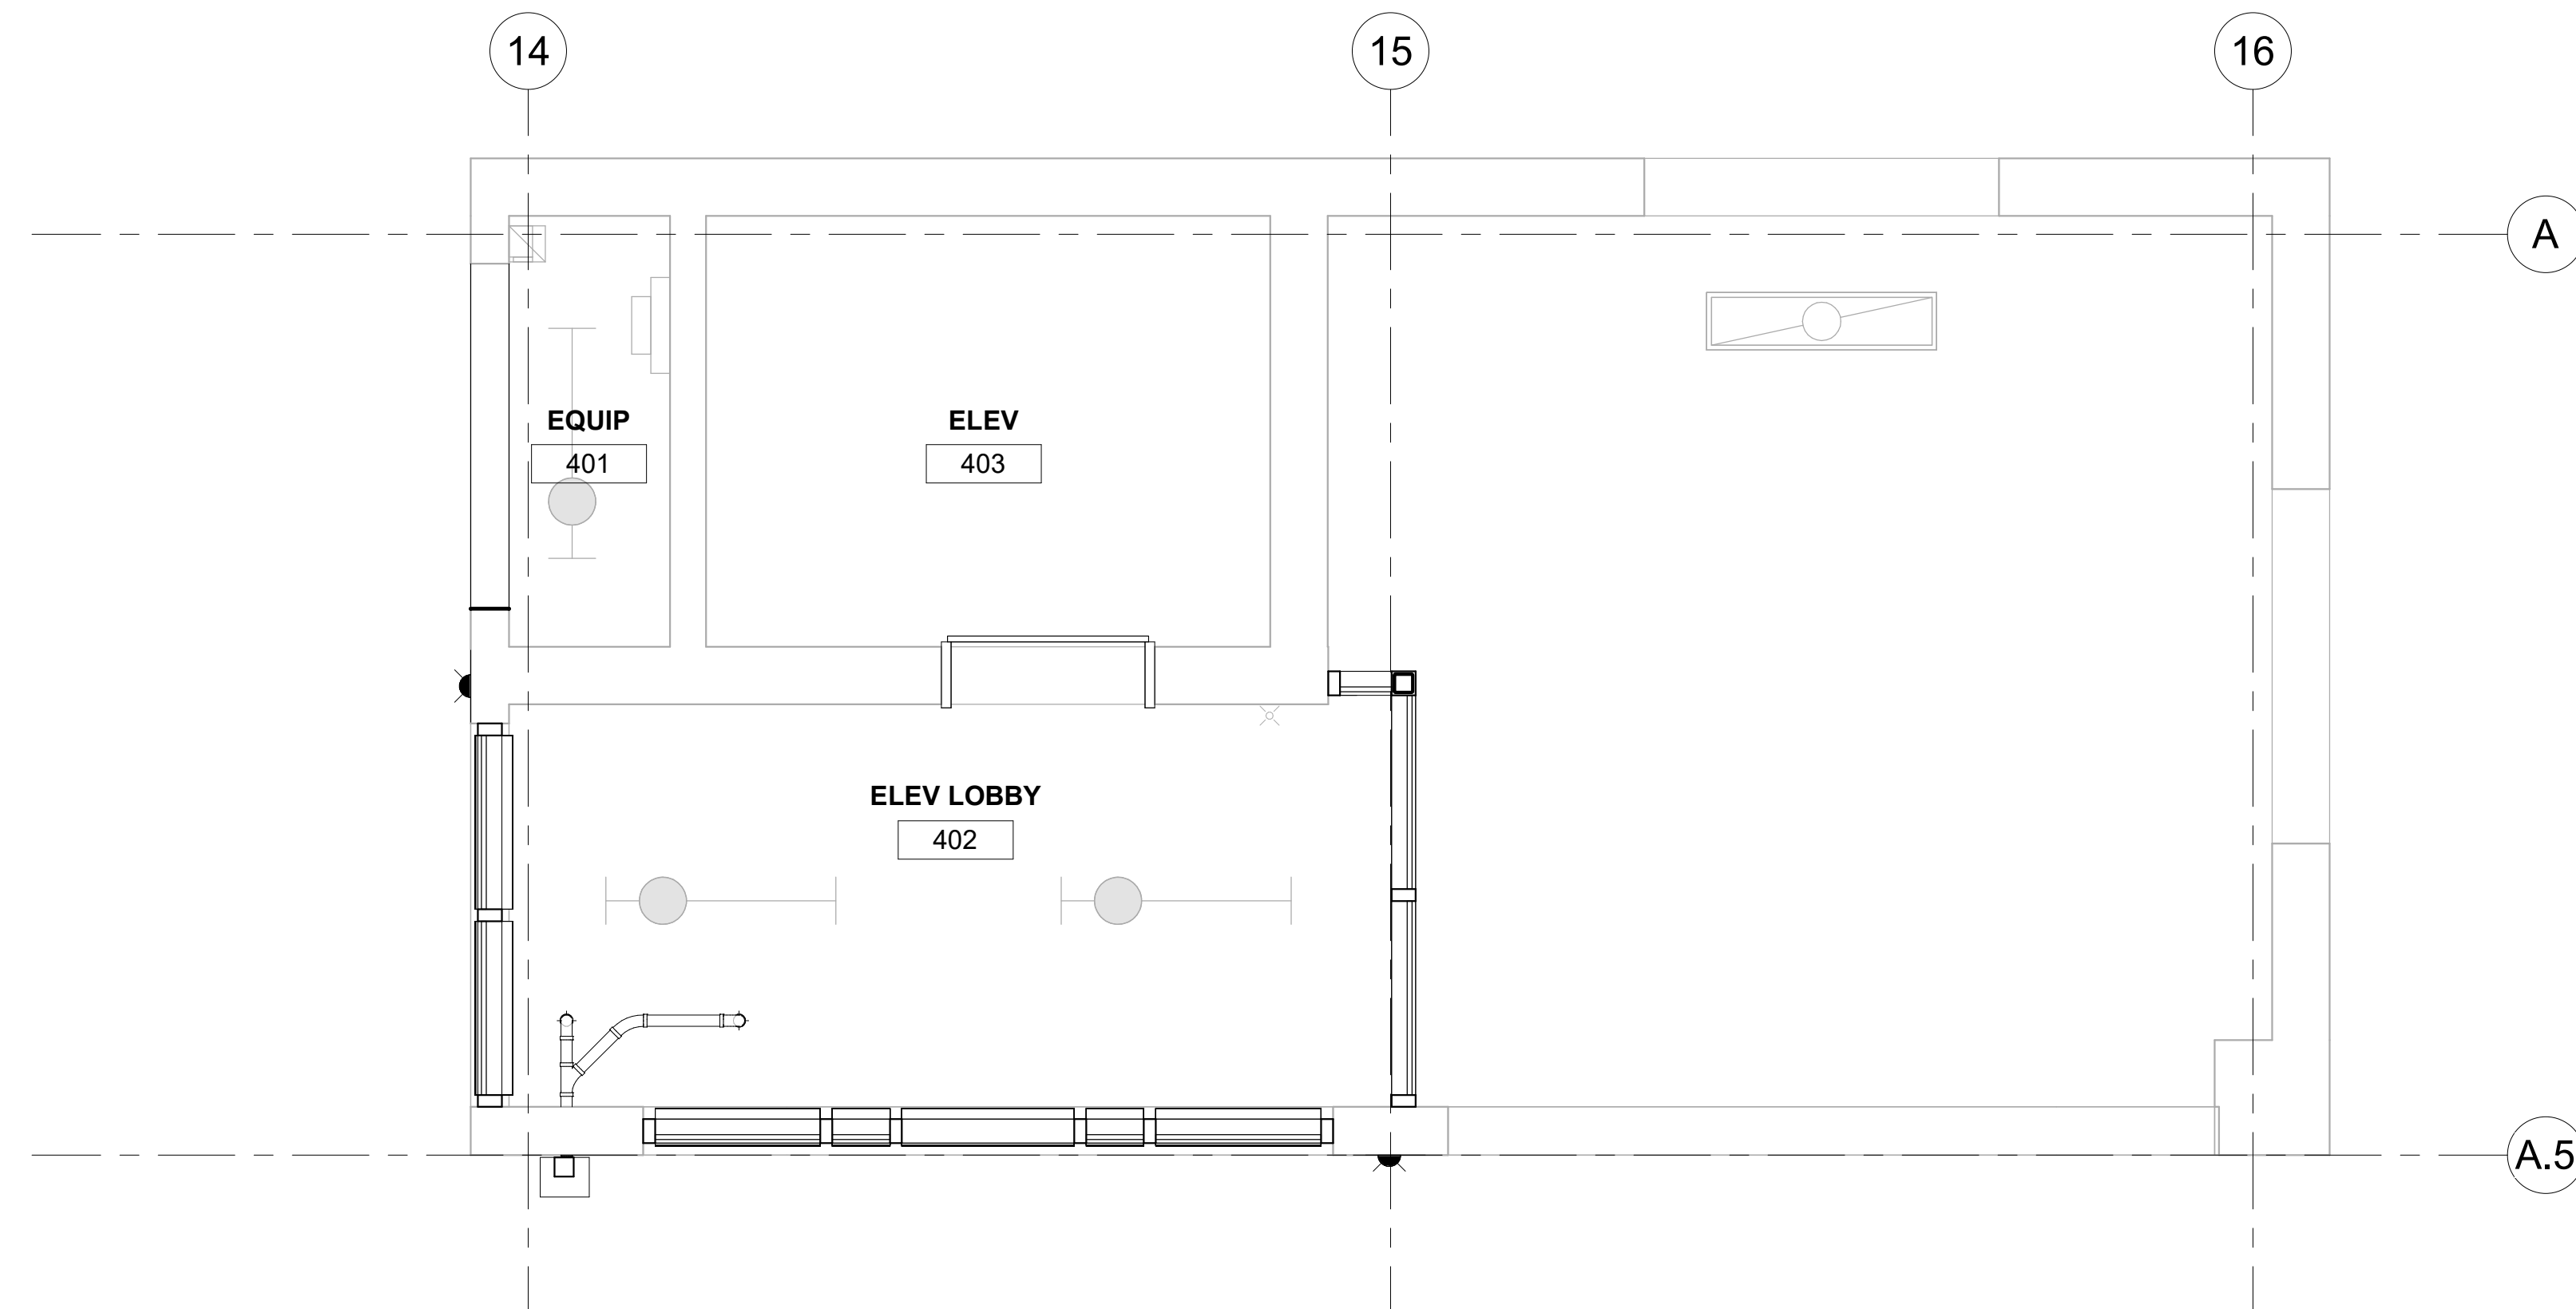

2 LEVEL 4 - ELEVATOR LOBBY - ENLARGED RCP
3/8" = 1'-0"

LEGEND

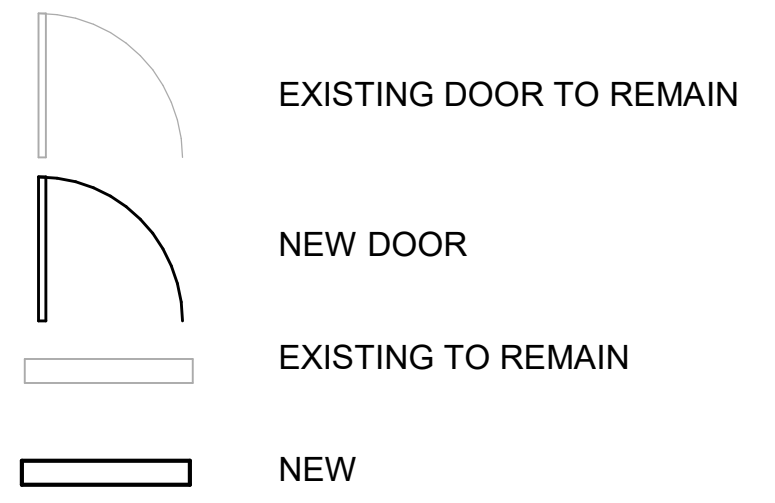


KEY NOTES (THIS SHEET ONLY)

F1	INSTALL NEW STAINLESS STEEL DOOR AND FRAME.
F2	SEE SHEET A-601 FOR SCOPE OF ELEVATOR WORK.
F3	INSTALL NEW ELEVATOR CAB DOOR.
F4	INSTALL NEW ALUMINUM STOREFRONT AND DOOR WITH THRESHOLD SET IN SEALANT.
F5	CLEAR RUST FROM STAINLESS STEEL JAMBS, TYP AT ALL FLOORS.
F6	CLEAN EXISTING CONCRETE DECK AT NEW ENCLOSED AREA.
F7	COMBINE EXISTING DOWNSPOUT AND OVERFLOW AND ROUTE THROUGH WALL TO NEW CONDUCTOR HEAD AND DOWNSPOUT. CORE DRILL THROUGH CONCRETE.
F8	NEW CONDUCTOR HEAD AND DOWNSPOUT.
F9	INSTALL NEW LIGHT IMPACT BOLLARDS.
F10	EXISTING BOLLARDS TO REMAIN.
F11	EXISTING OPENING.
F12	NEW STRUCTURAL MEMBER, SEE STRUCTURAL.

GENERAL NOTES

- DIMENSIONS SHOWN ARE FROM GRID LINES TO FACE OF STUD, CENTERLINE OF STRUCTURAL COLUMNS, CENTERLINE OF OPENINGS, UNO.
- ANY DOORS NOT DIMENSIONED SHALL BE INSTALLED 6" FROM THE INTERSECTING WALL OR CENTERED ON THE WALL, UNO.
- ALL DIMENSIONS NOTED AS CLEAR SHALL MAINTAIN THE FULL SPACE INDICATED WITHOUT ENCROACHMENTS.
- ENSURE THAT ALL REQUIRED BACKING IS INSTALLED IN WALLS PRIOR TO INSTALLING GYPSUM BOARD.

KEY PLAN

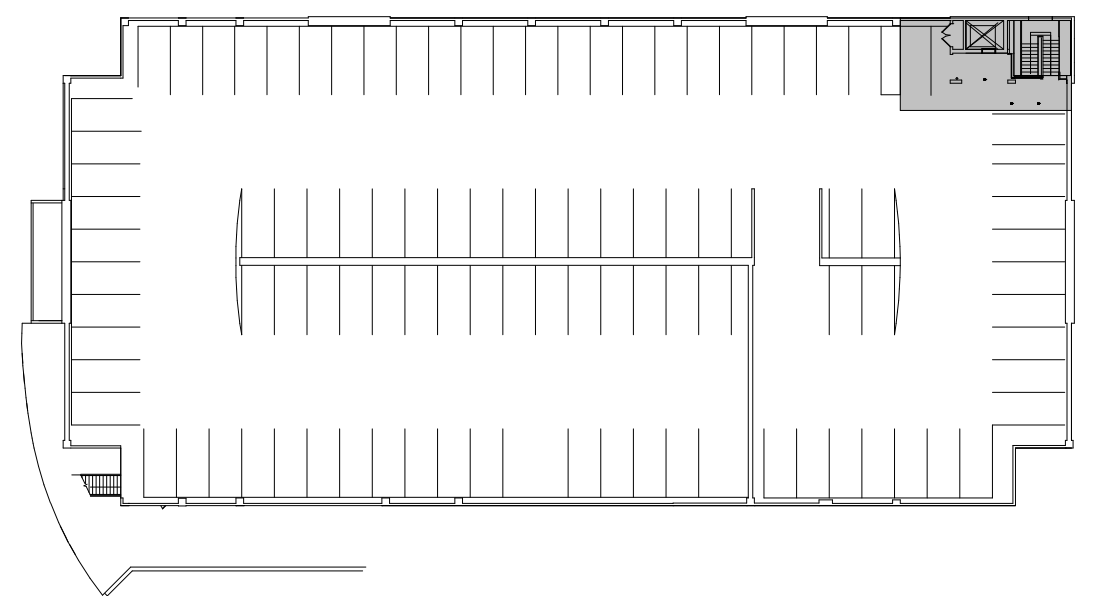

AREA SHOWN

--	--	

A

B

C

D

E

F

A


B

C


D

E


F

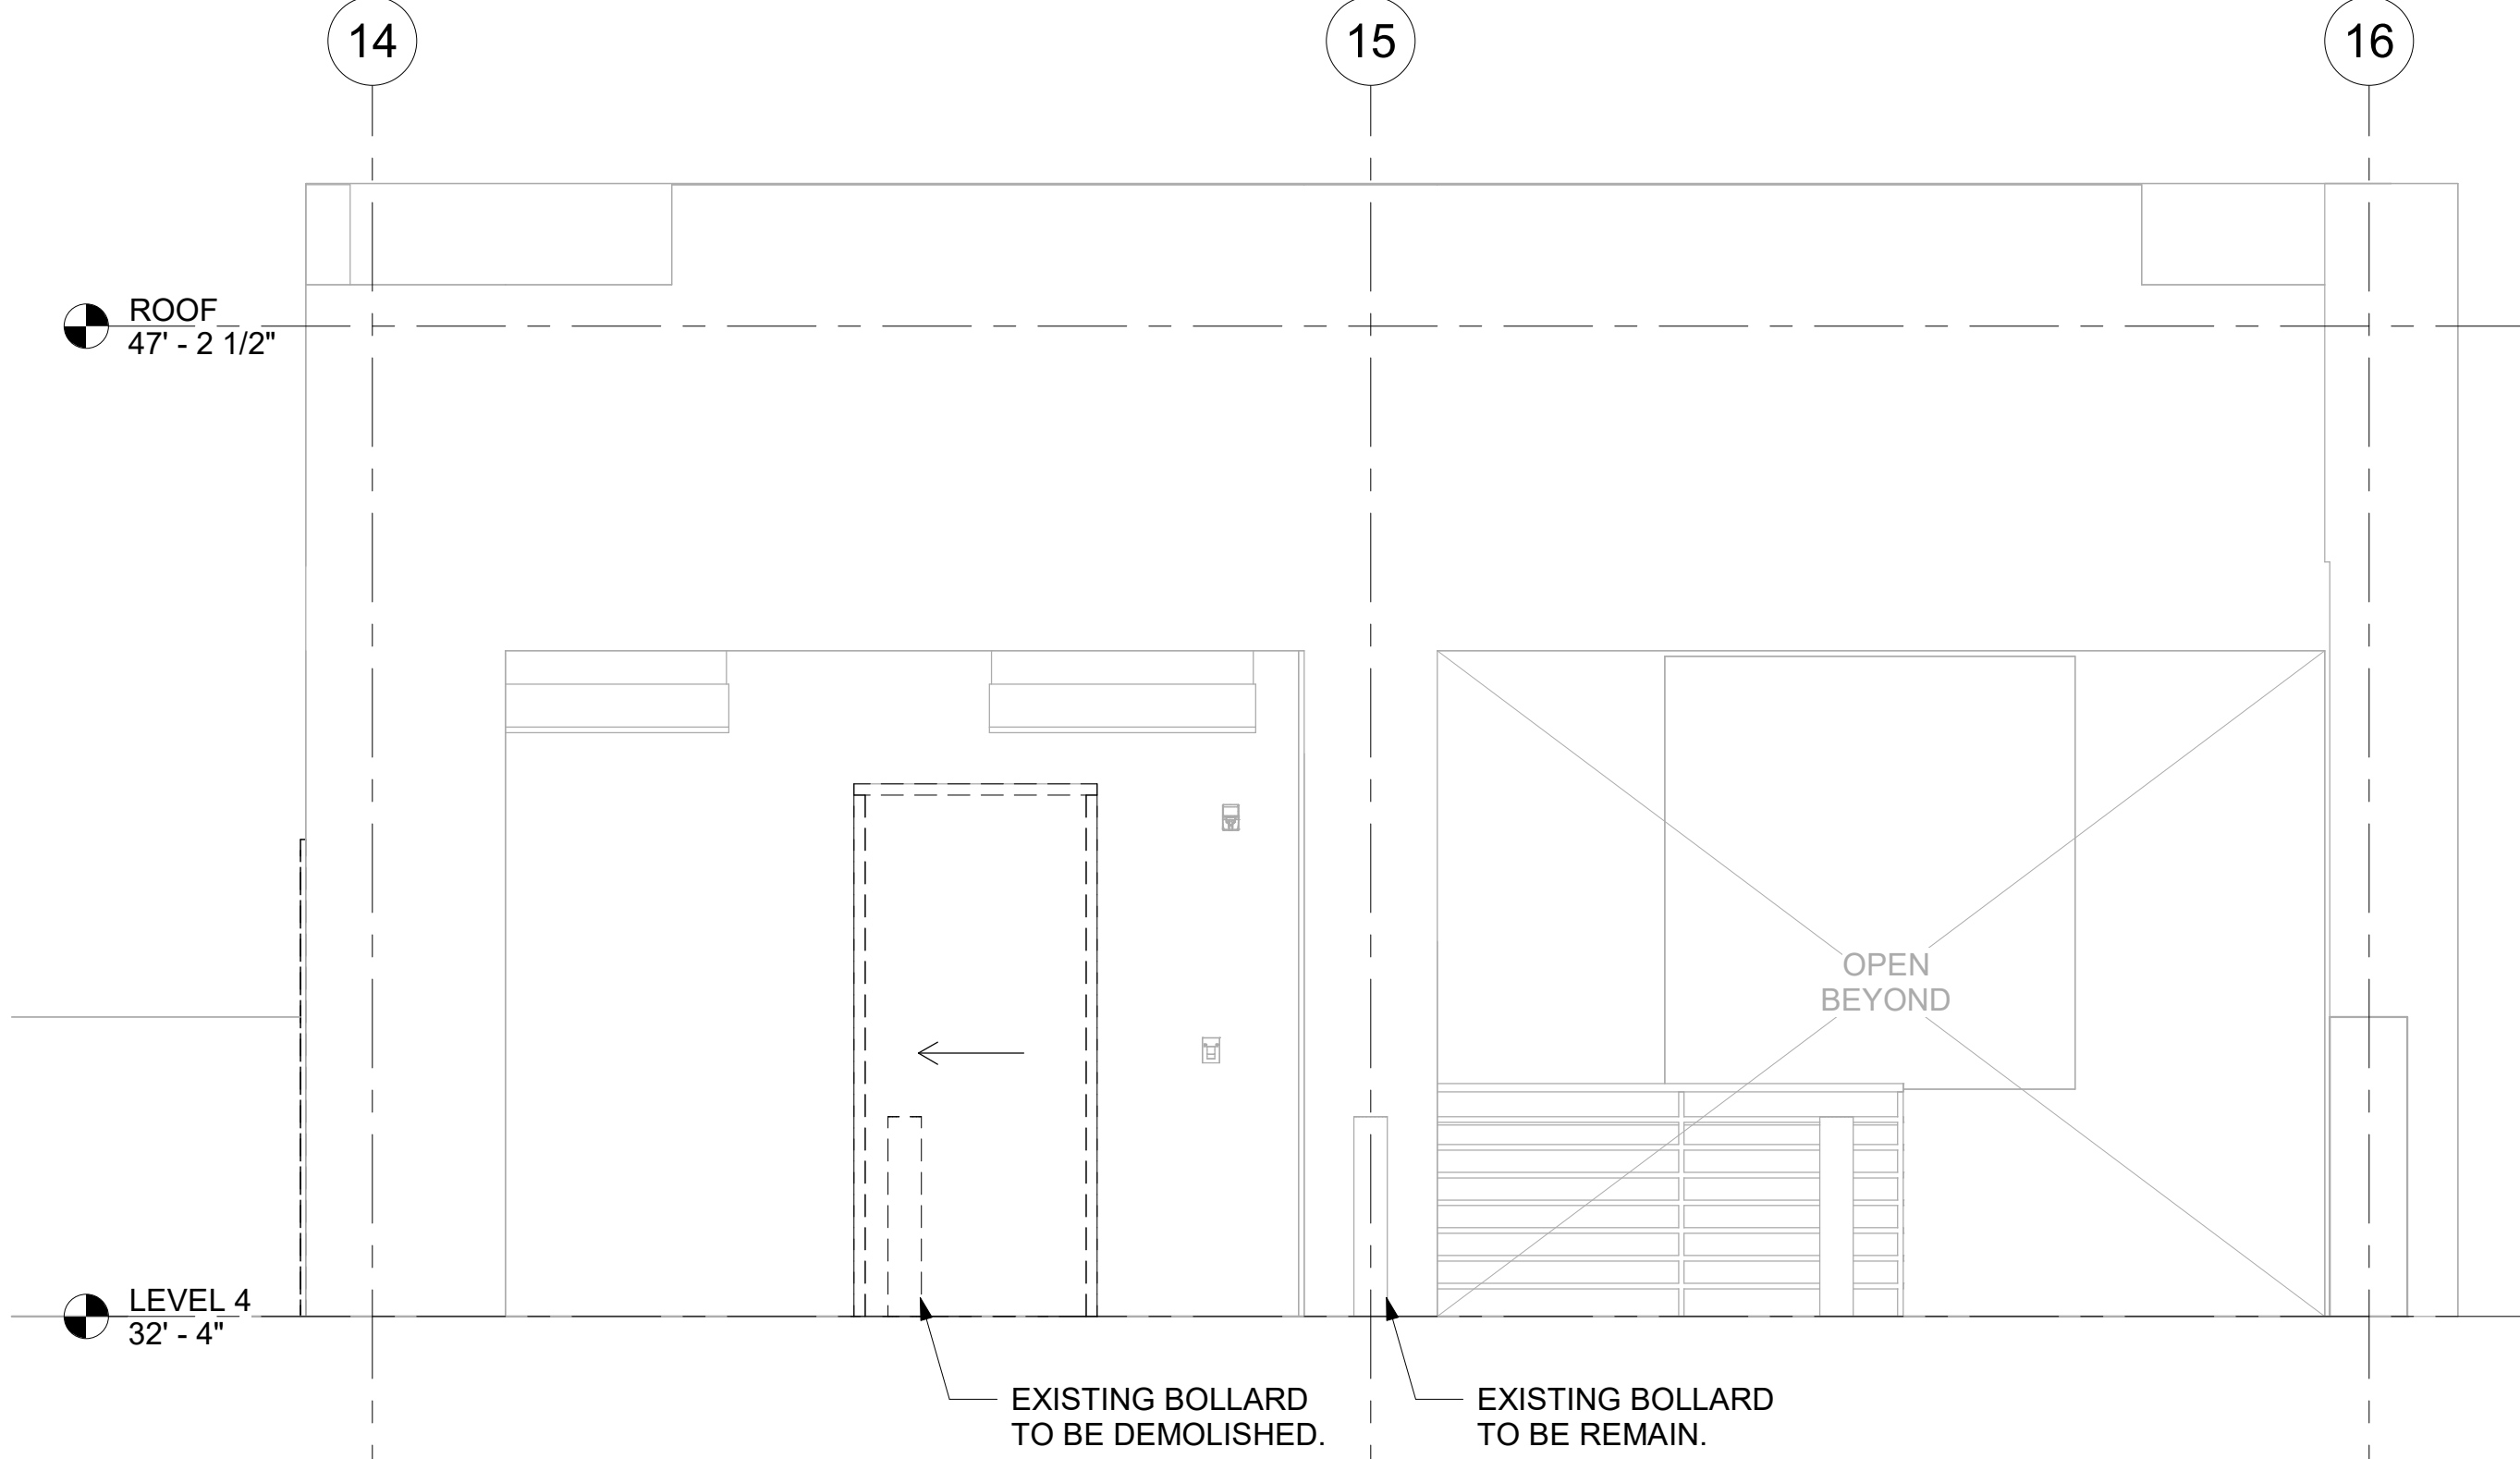


1 ELEVATOR LOBBY - SOUTH ELEVATION - EXISTING CONDITIONS
3/8" = 1'-0"

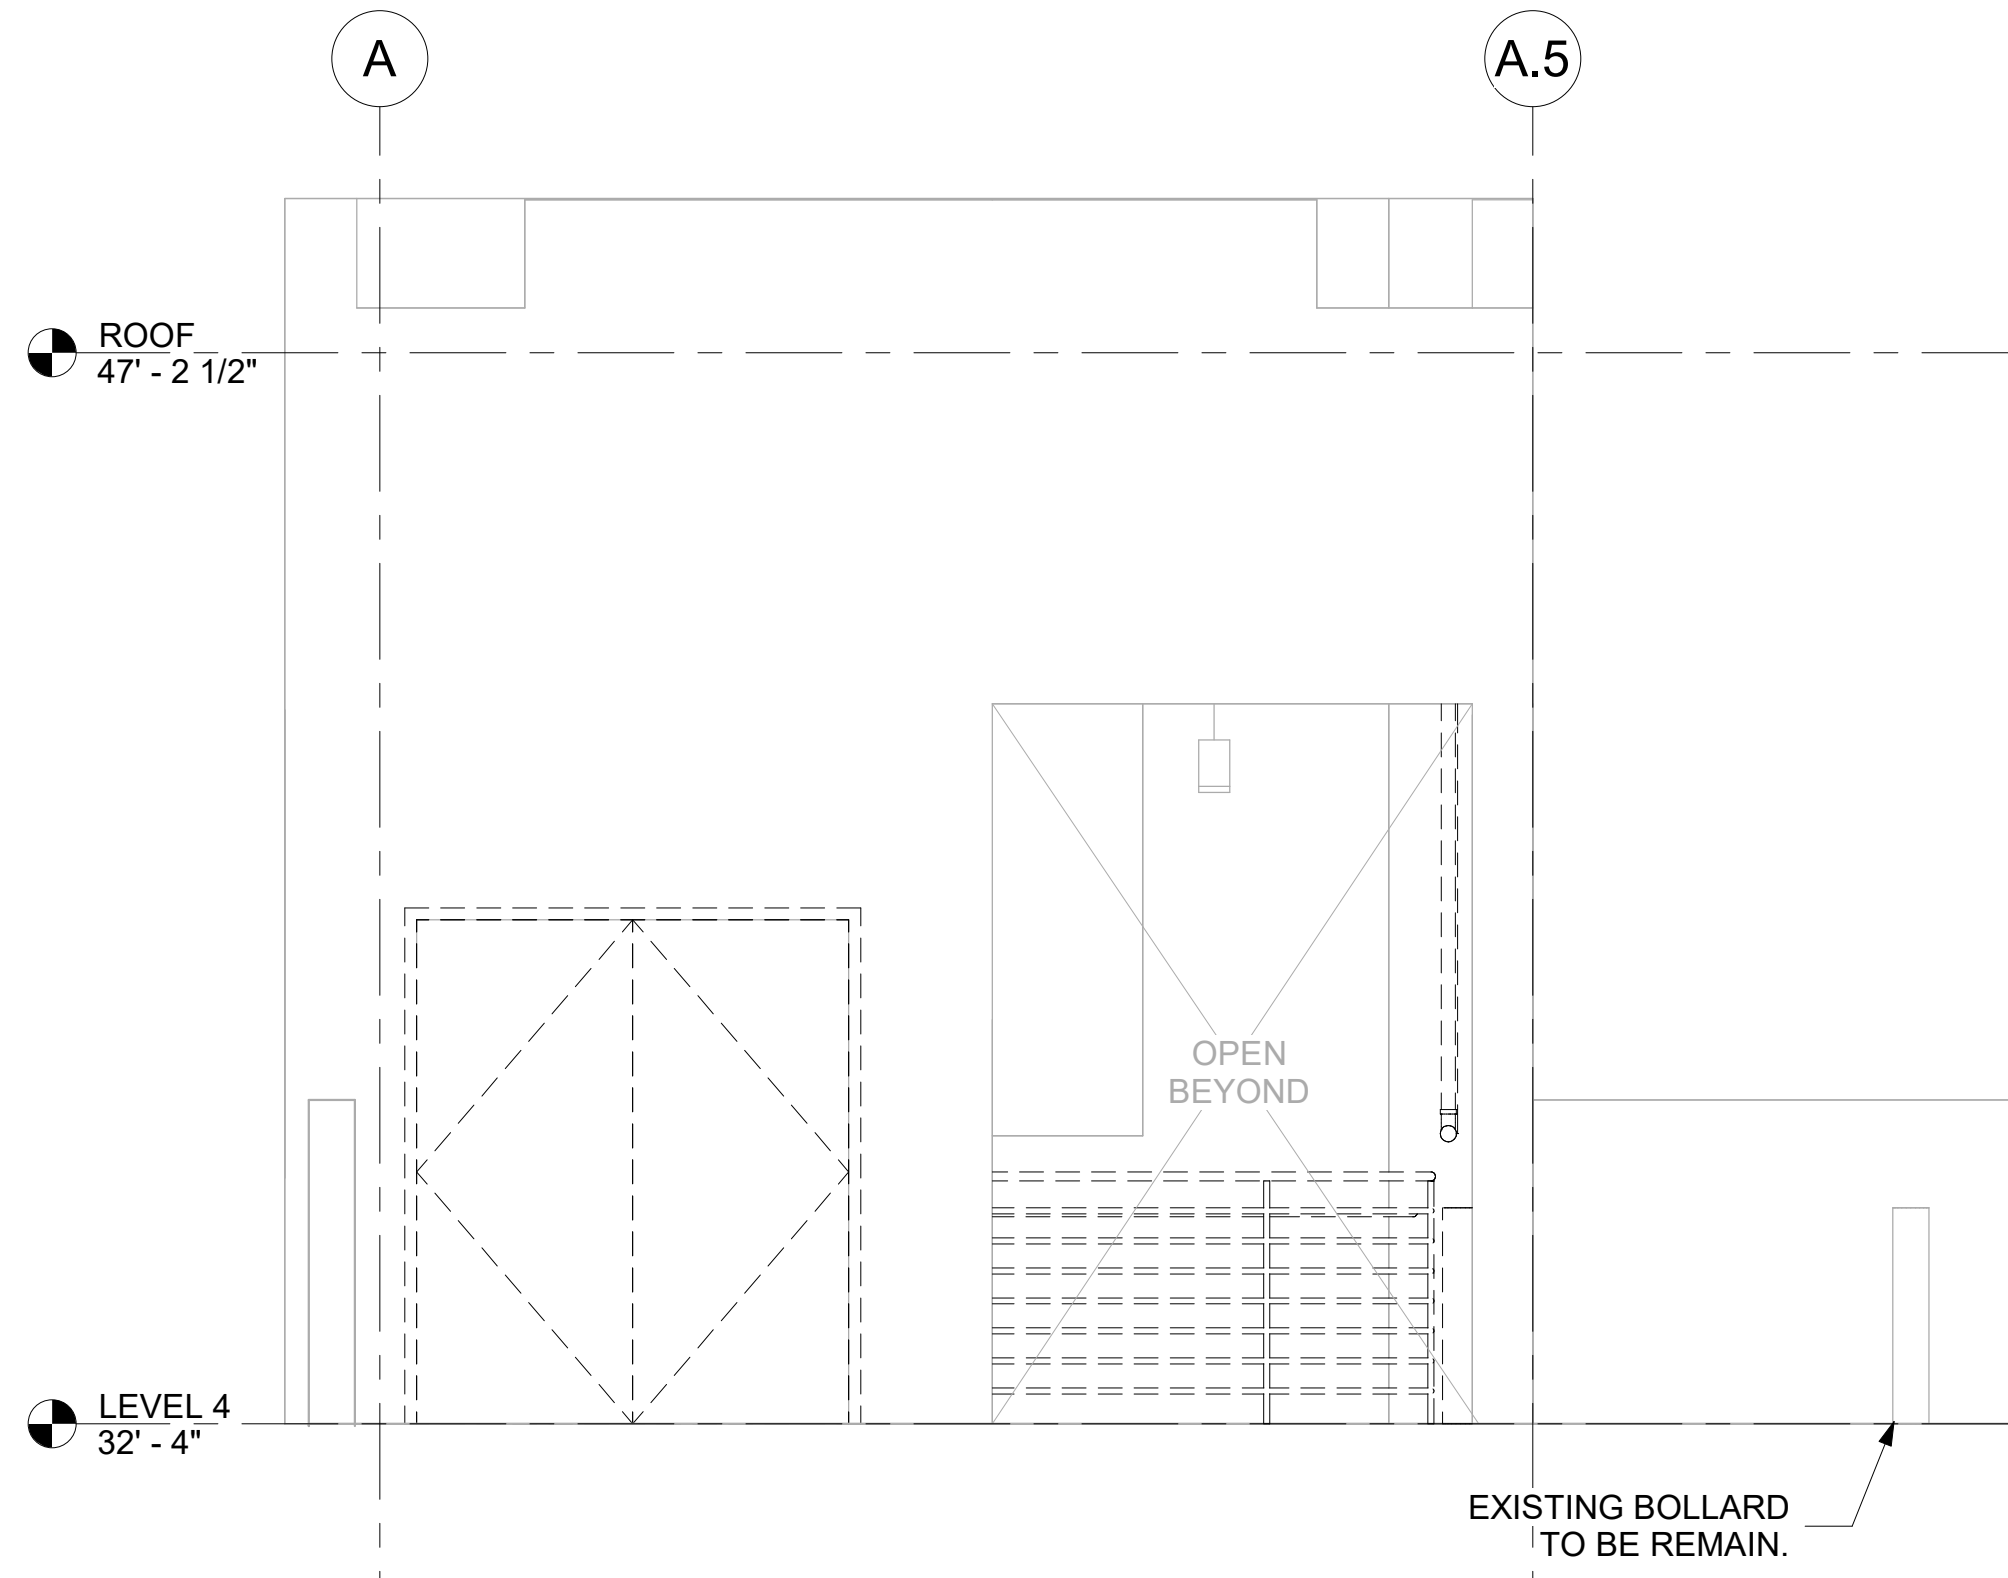


2 ELEVATOR LOBBY - WEST ELEVATION - EXISTING CONDITIONS
3/8" = 1'-0"

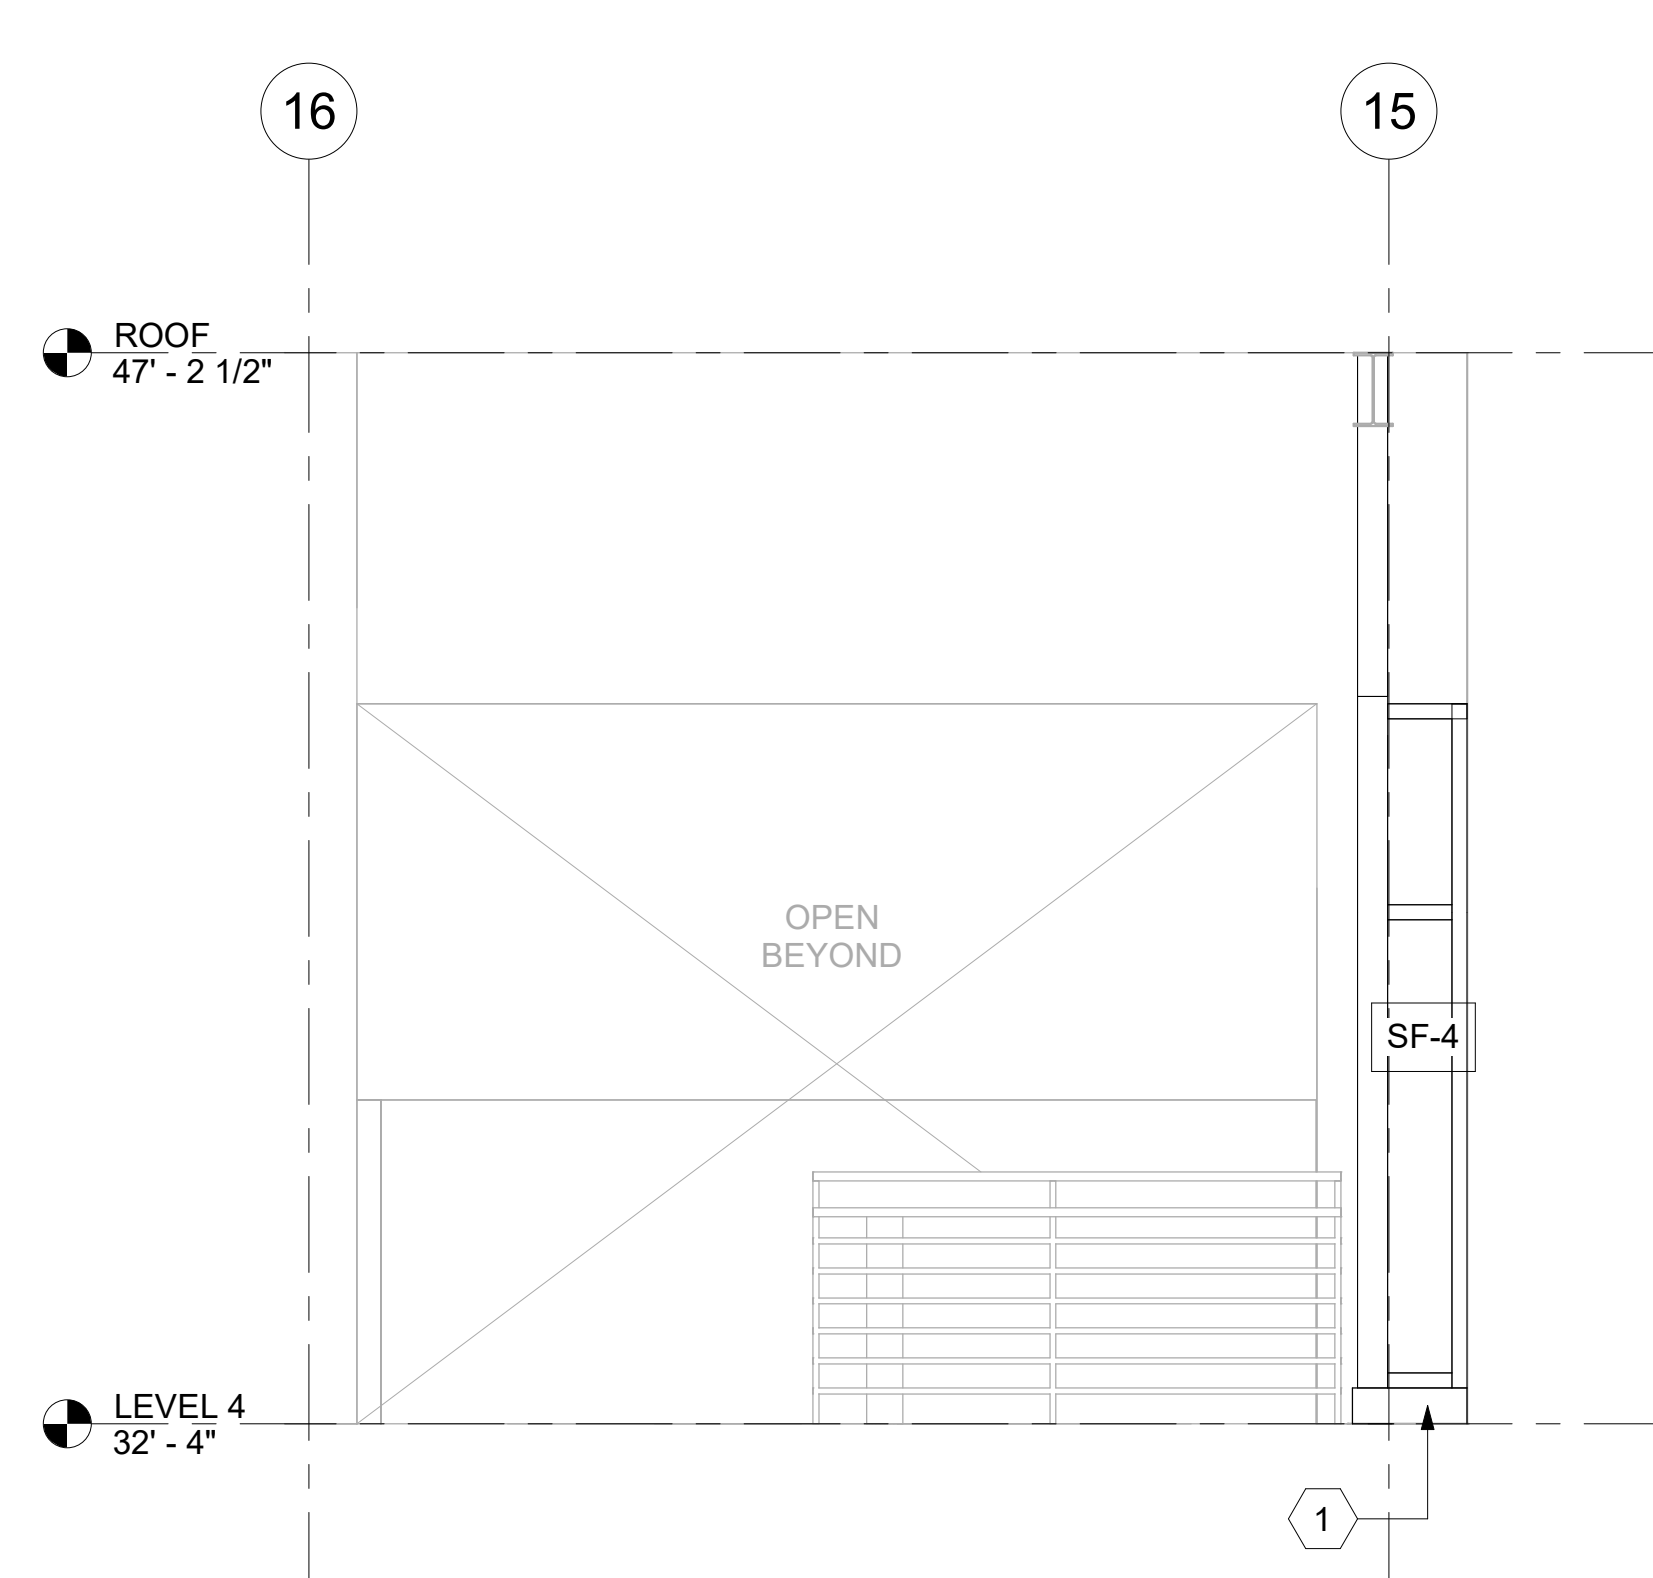


3 ELEVATOR LOBBY - SOUTH INTERIOR ELEVATION
3/8" = 1'-0"

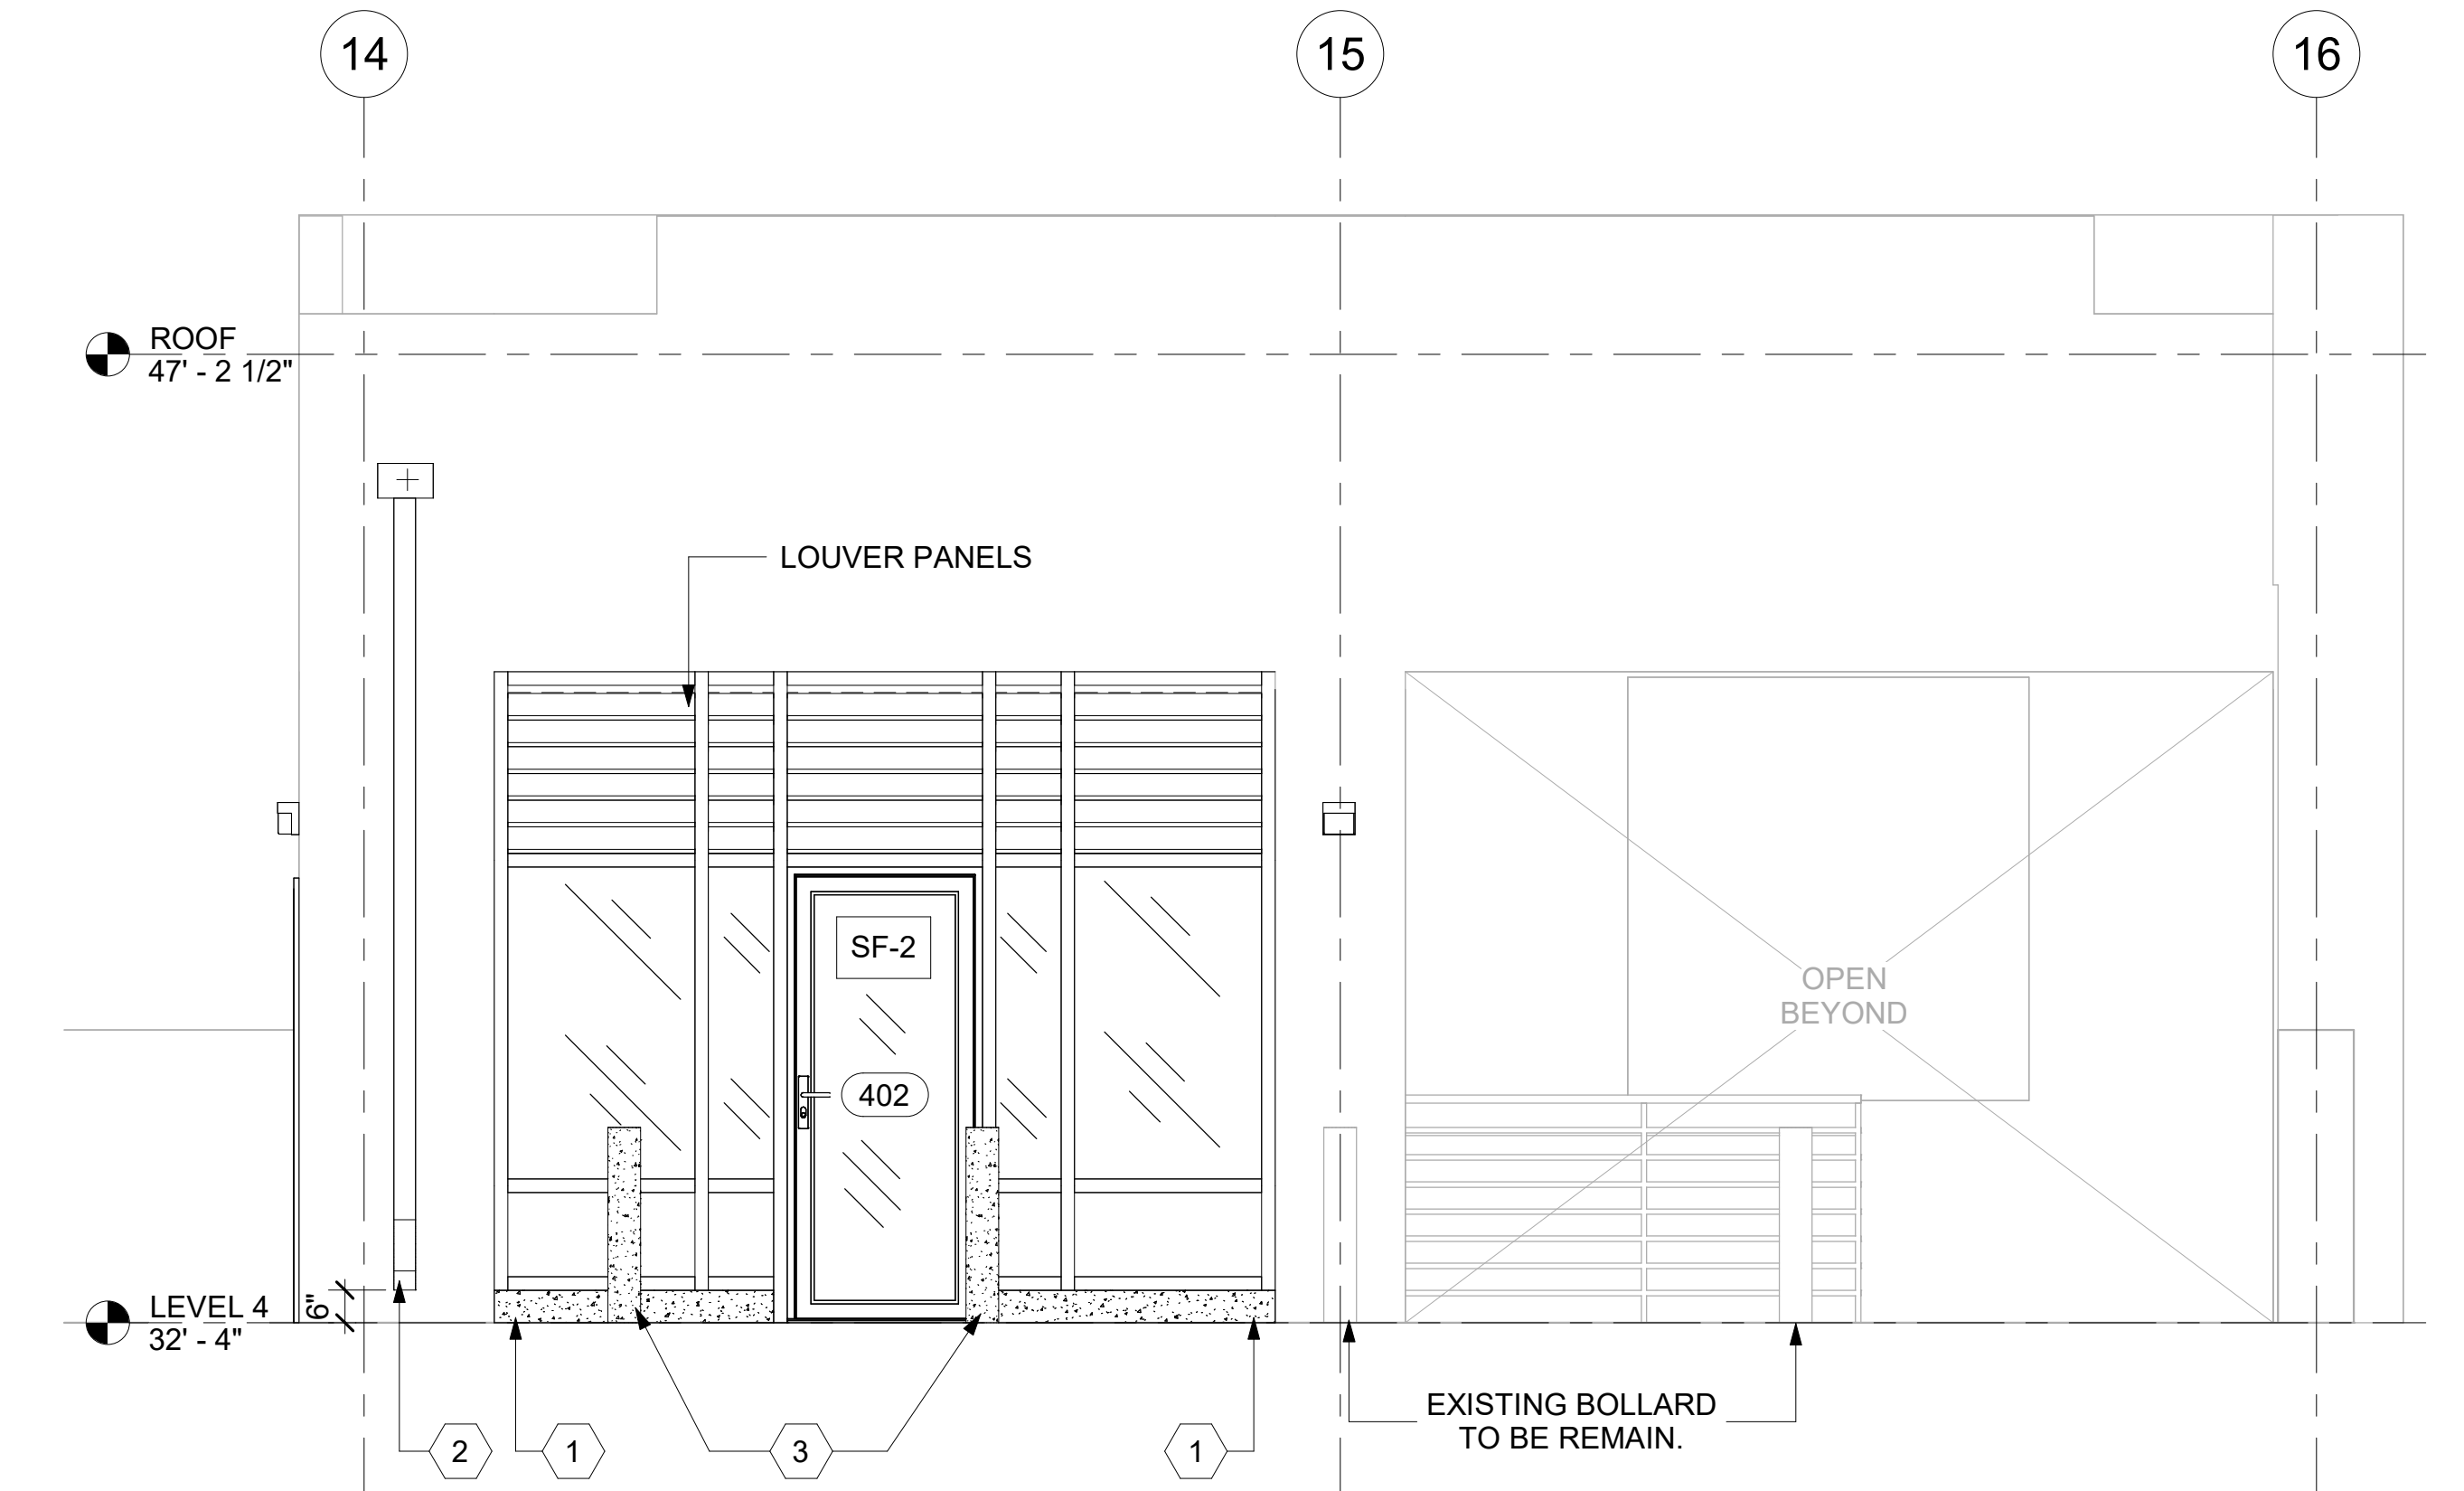

4 ELEVATOR LOBBY - SOUTH ELEVATION
3/8" = 1'-0"

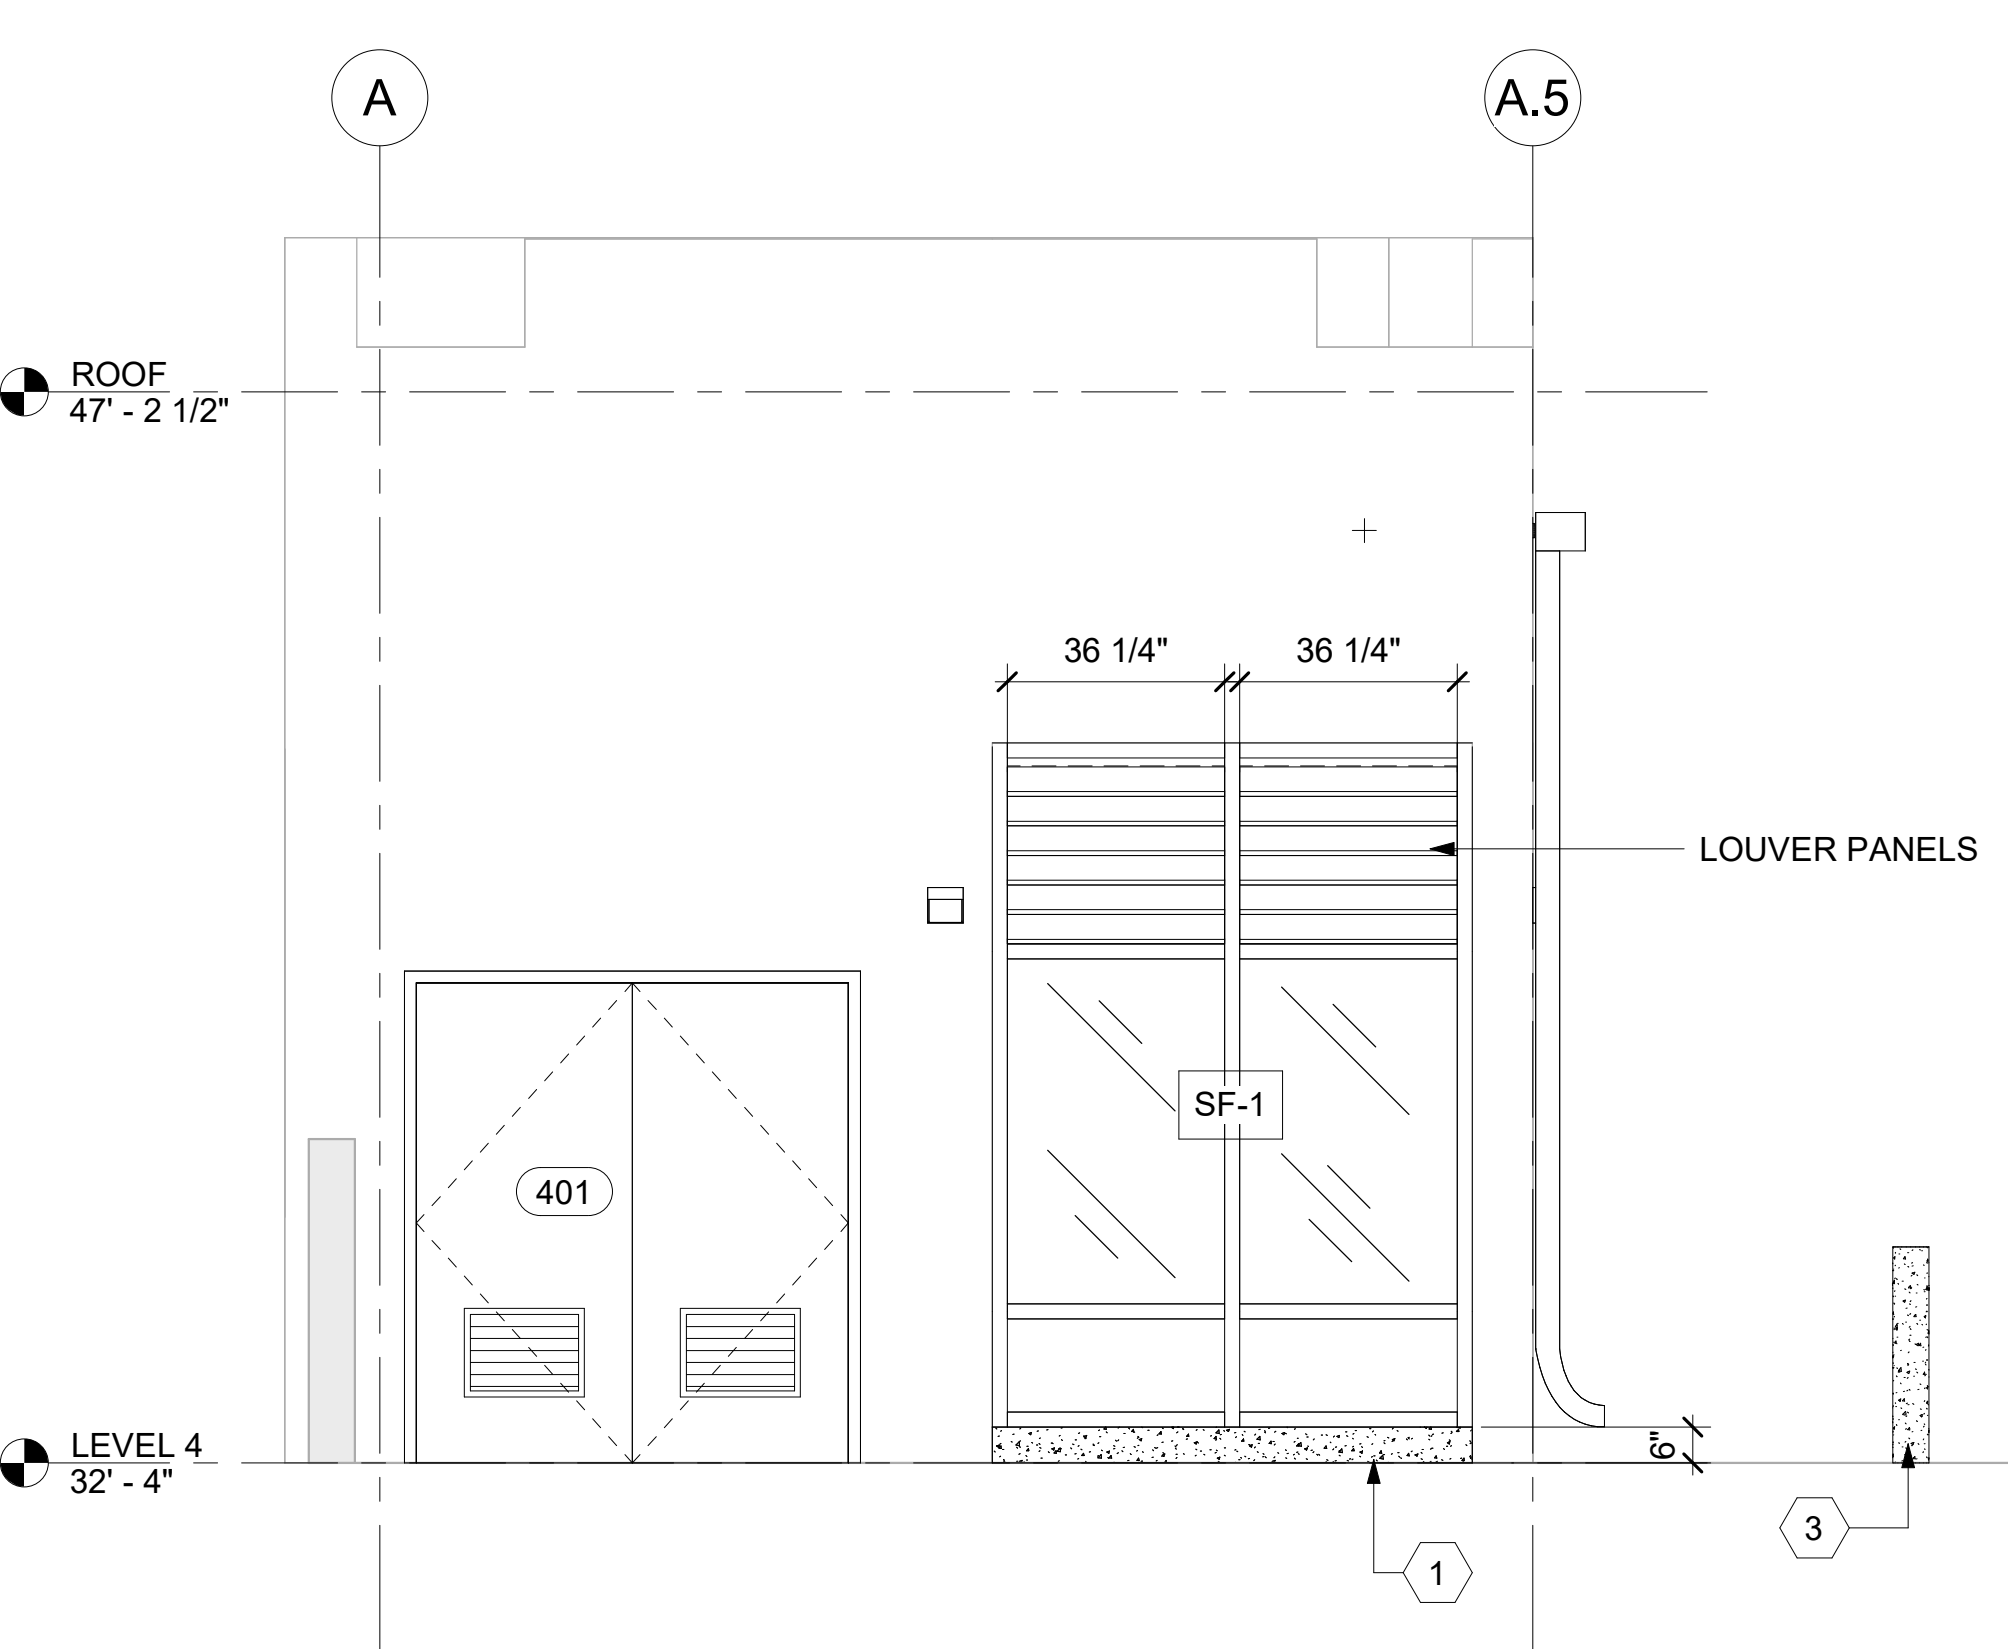

5 ELEVATOR LOBBY - WEST ELEVATION
3/8" = 1'-0"

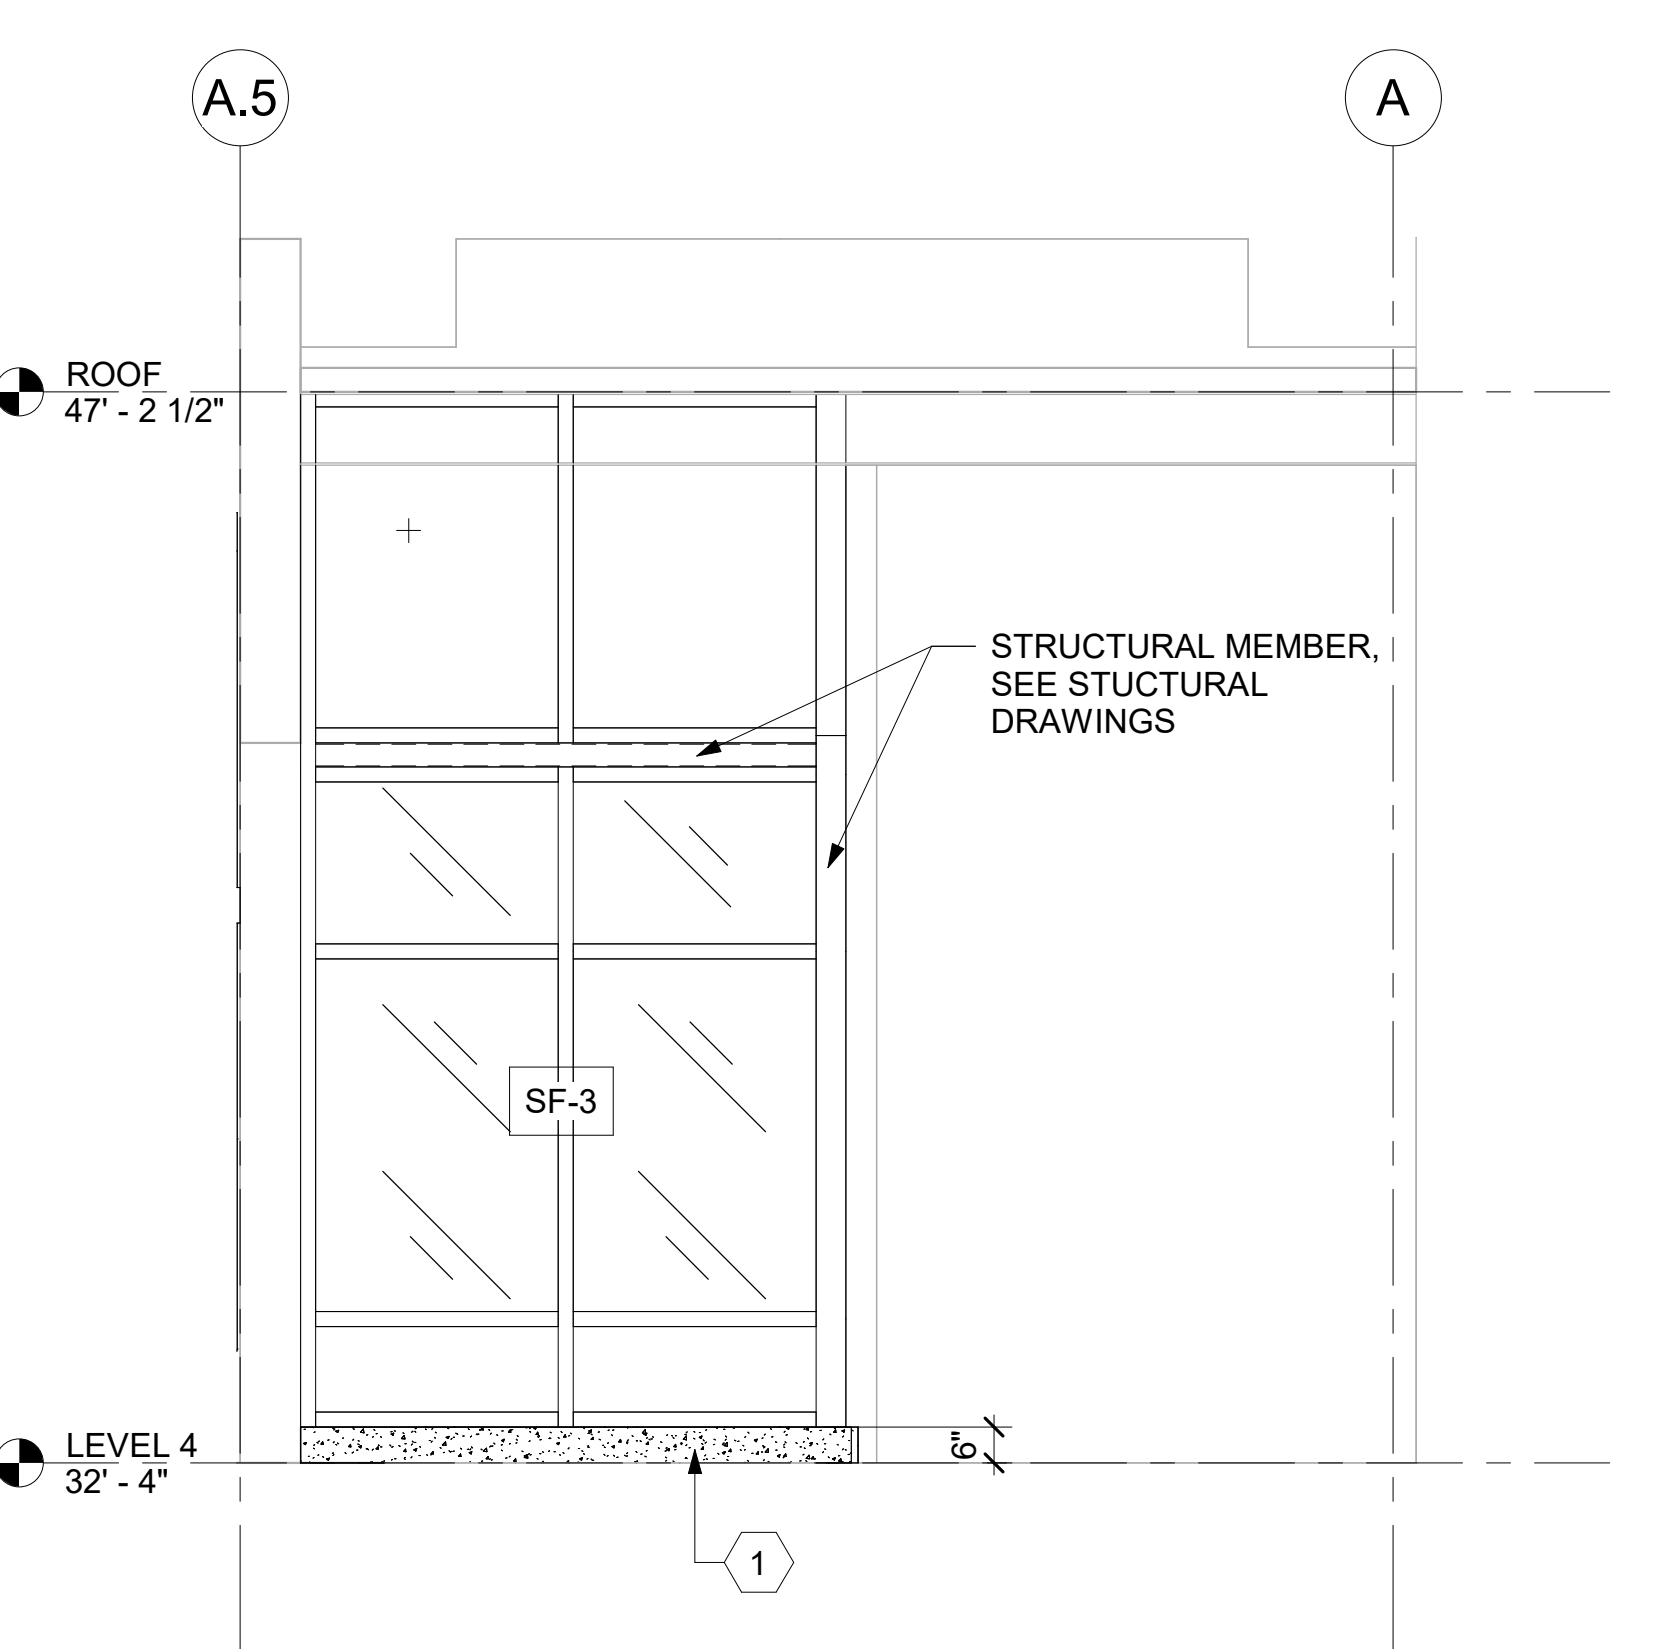

6 ELEVATOR LOBBY - EAST ELEVATION
3/8" = 1'-0"

KEY NOTES (THIS SHEET ONLY)

1	NEW CONCRETE CURB.
2	NEW STAINLESS STEEL METAL CONDUCTOR HEAD AND DOWNSPOUT.
3	NEW BOLLARD.

GENERAL NOTES

- INDICATED MOUNTING HEIGHTS COMPLY WITH ARCHITECTURAL BARRIER ACT (ABA) ACCESSIBILITY STANDARDS, 2004, INCLUDING VA SUPPLEMENT BARRIER FREE DESIGN STANDARD (PG18-13), REV 2024.
- VA FURNISHED, VA INSTALLED EQUIPMENT IS SHOWN WITH HALF-TONED GRAY LINEWORK FOR CLARITY. SEE SPECIALTY EQUIPMENT SCHEDULE.
- ALL WALL MOUNTED EQUIPMENT SHALL HAVE METAL BLOCKING IN WALL BEHIND. ENSURE ALL REQUIRED BACKING IS INSTALLED PRIOR TO INSTALLING DRYWALL. SEE TYPICAL BLOCKING DETAIL.
- ALL VERTICAL HEIGHTS INDICATED ARE FROM THE FINISH FLOOR ELEVATION, UNO.

Revisions:	Date:

CONSULTANT
ENGINEERING DISCIPLINE:

ARCHITECT/ENGINEER OF RECORD
A/E:
SPEES DESIGN BUILD
23830 PACIFIC HIGHWAY S, SUITE 300
KENT, WA 98032



Office of
Capital Projects
VA U.S. Department
of Veterans Affairs

Drawing Title
EXTERIOR ELEVATIONS

Approved:

Phase
100% CONSTRUCTION
DOCUMENTS

Project Title
REPAIR AND WEATHERIZE
PARKING STRUCTURE 211
ELEVATOR

Location
SAN FRANCISCO VA MEDICAL CENTER - SAN
FRANCISCO, CA

Issue Date
11/17/2025


Checked
MK

Drawn
AJ


Project Number
662-23-111
Building Number
211

Drawing Number
AE420


ELEVATOR SCOPE OF WORK			
MACHINE ROOM	DESCRIPTION	ACTION REQUIRED	COMMENTS
MACHINE TYPE/MFR.	GEARLESS IMPERIAL	RETAIN, PROVIDE NEW HOIST ROPES.	CLEAN/INSPECT/SERVICE
SEISMIC CONTROL	RING & STING	PROVIDE NEW	
GOVERNORS	HW207	PROVIDE NEW	NEW GOV ROPE
LIGHTING	FLUORESCENT	PROVIDE NEW	
110V OUTLET GFCI	YES	PROVIDE NEW	
HOISTWAY	DESCRIPTION	ACTION REQUIRED	COMMENTS
DO MFR/MODEL	WEATHER-RESISTANT GAL OPERATOR	PROVIDE NEW	
RESTRICTOR	WEATHER-RESISTANT GAL OPERATOR	PROVIDE NEW	
CAR DOOR HANGERS	WEATHER-RESISTANT GAL OPERATOR	PROVIDE NEW	
DOOR PROTECTION	INFRARED	PROVIDE NEW	
HALL DOOR HANGERS	WEATHER-RESISTANT GAL OPERATOR	PROVIDE NEW	
CLOSER TYPE	SPIRATOR	PROVIDE NEW	SMARTORK
CAR GUIDES	ELSCO ADJ. SPRINT ROLLER	CLEAN/REMOVE RUST	
CAR GUIDE RAILS	ELSCO ADJ. SPRINT ROLLER	CLEAN/REMOVE RUST	
COUNTERWEIGHT RAILS			
PIT	DESCRIPTION	ACTION REQUIRED	COMMENTS
BUFFERS	SPRING	CLEAN/REPAINT	
CAB ENCLOSURE	DESCRIPTION	ACTION REQUIRED	COMMENTS
ENTRANCE FINISH	#4 STAINLESS STEEL	RECONDITION STAINLESS STEEL	
FRONT RETURN	#4 STAINLESS STEEL	RECONDITION STAINLESS STEEL	
DOORS	#4 STAINLESS STEEL	NEW STAINLESS STEEL DOORS	4TH FLOOR ONLY
TRANSOM	#4 STAINLESS STEEL	RECONDITION STAINLESS STEEL	
WALL FINISH	STAINLESS STEEL PANELS	RECONDITION STAINLESS STEEL	
SHELL	STEEL	PROVIDE NEW LID	
CEILING	STAINLESS STEEL PANELS	CLEAN	
ENTRANCES	DESCRIPTION	ACTION REQUIRED	COMMENTS
FOURTH FLOOR DOORS	STAINLESS	REPLACE	
FOURTH FLOOR FRAMES	STAINLESS	REFINISH	
FOURTH FLOOR SILL	ALUMINUM	CLEAN	
SIGNAL FIXTURES	DESCRIPTION	ACTION REQUIRED	COMMENTS
HALL STATIONS/FINISH	#4 STAINLESS STEEL	PROVIDE NEW	4TH FLOOR ONLY
HALL PI LOCATION	OVER ENTRANCE AT EACH FLOOR	PROVIDE NEW DIGITAL PI/HL	4TH FLOOR ONLY
HOISTWAY ACCESS	KEYED TOP AND BOTTOM	PROVIDE NEW	

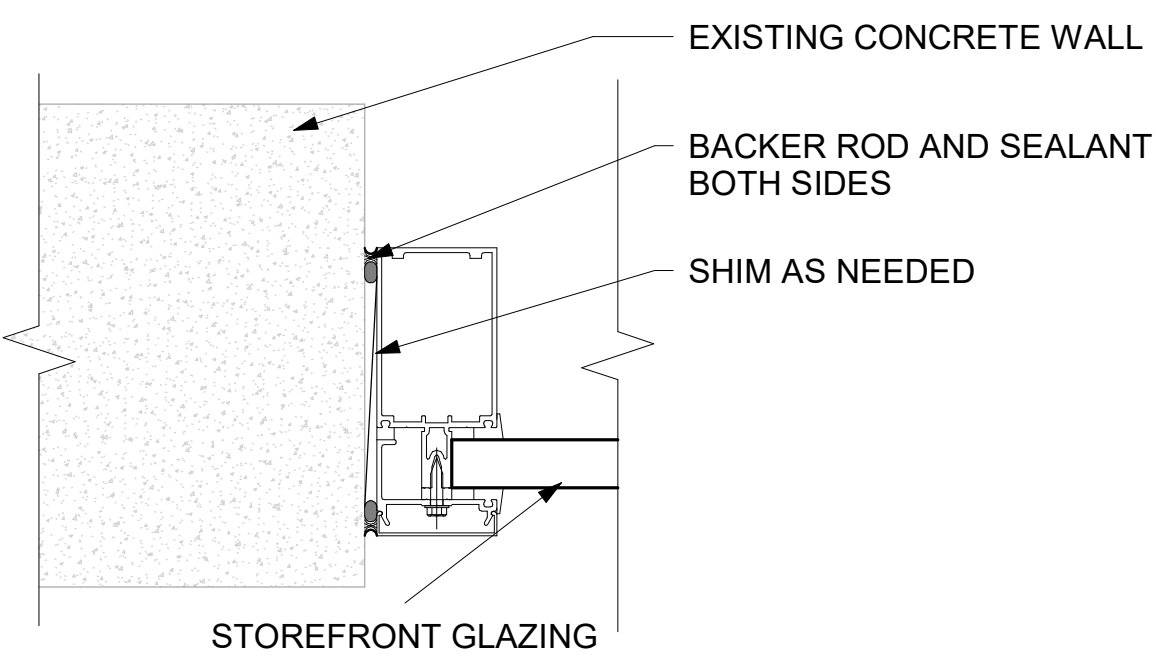


2 STOREFRONT JAMB DETAIL
3" = 1'-0"

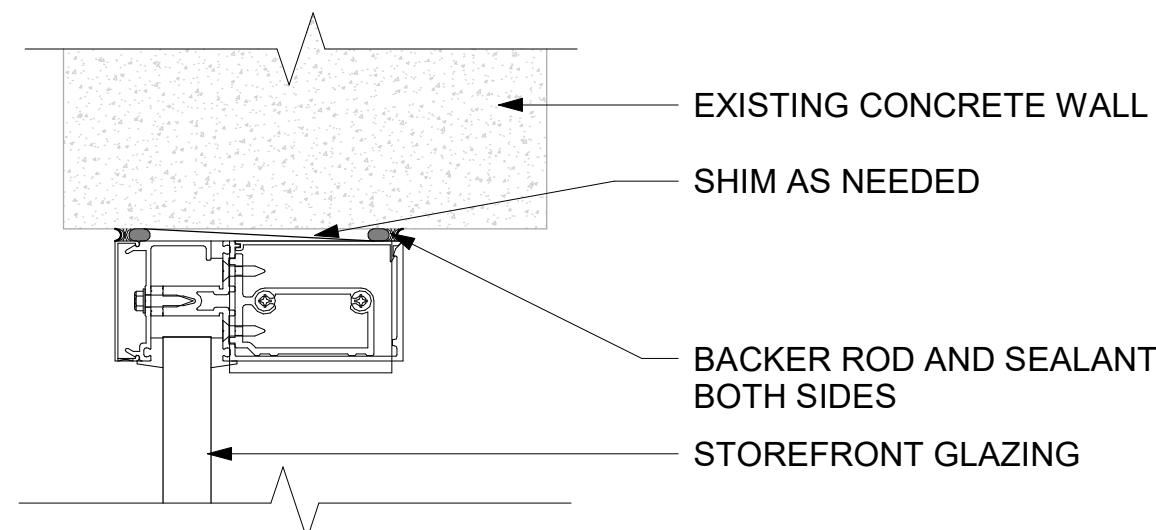


3 STOREFRONT HEAD DETAIL
3" = 1'-0"

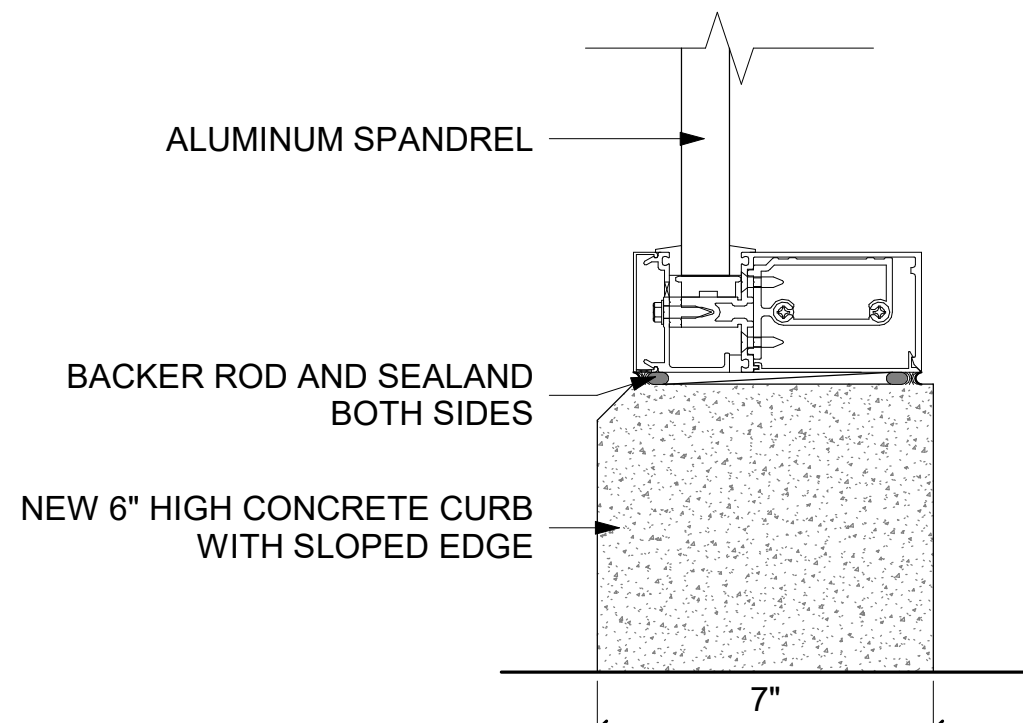



5 STOREFRONT SILL DETAIL
3" = 1'-0"

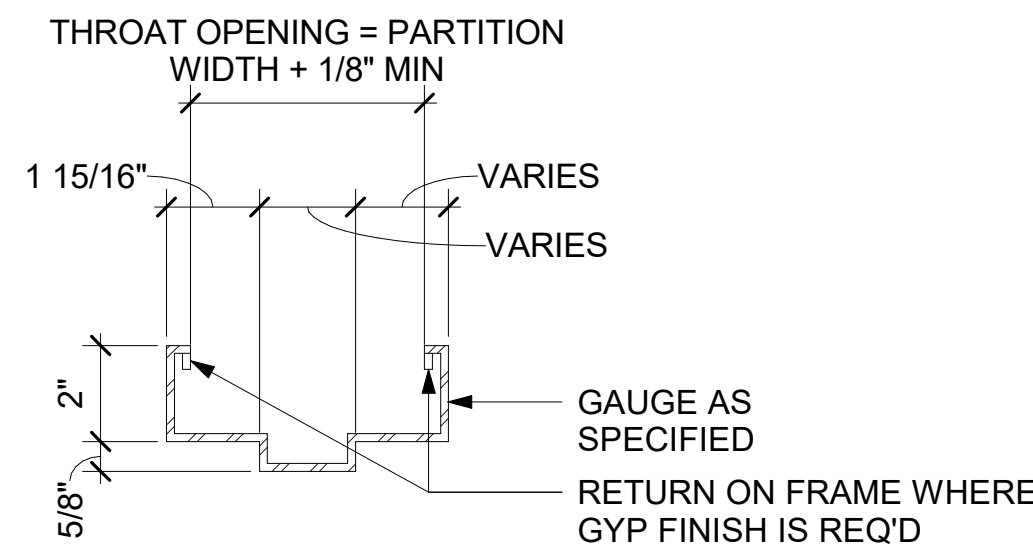

6 STANDARD DOOR FRAME
3" = 1'-0"

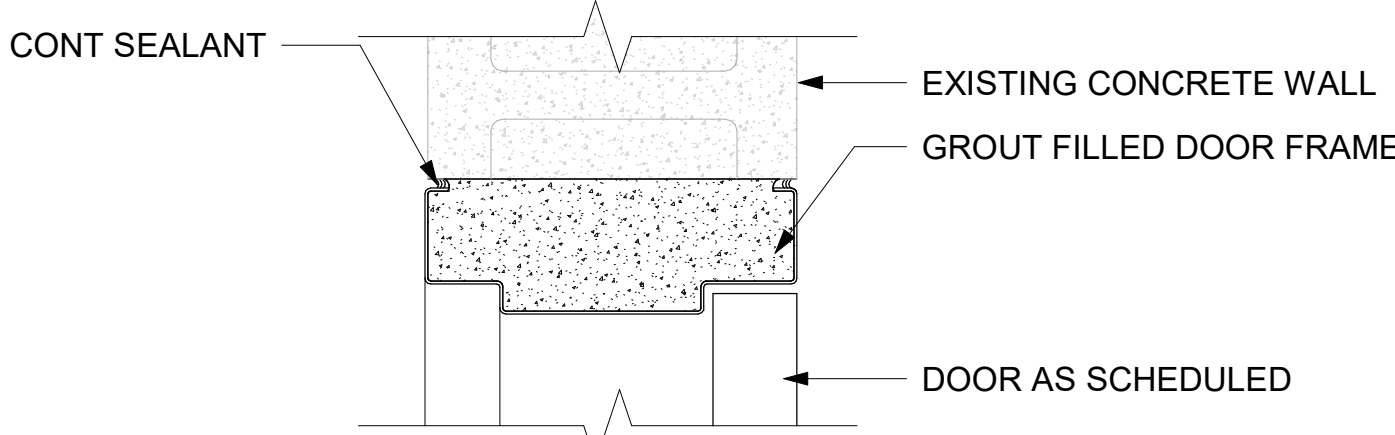

7 FRAMES @ EXISTING CONCRETE WALL
3" = 1'-0"

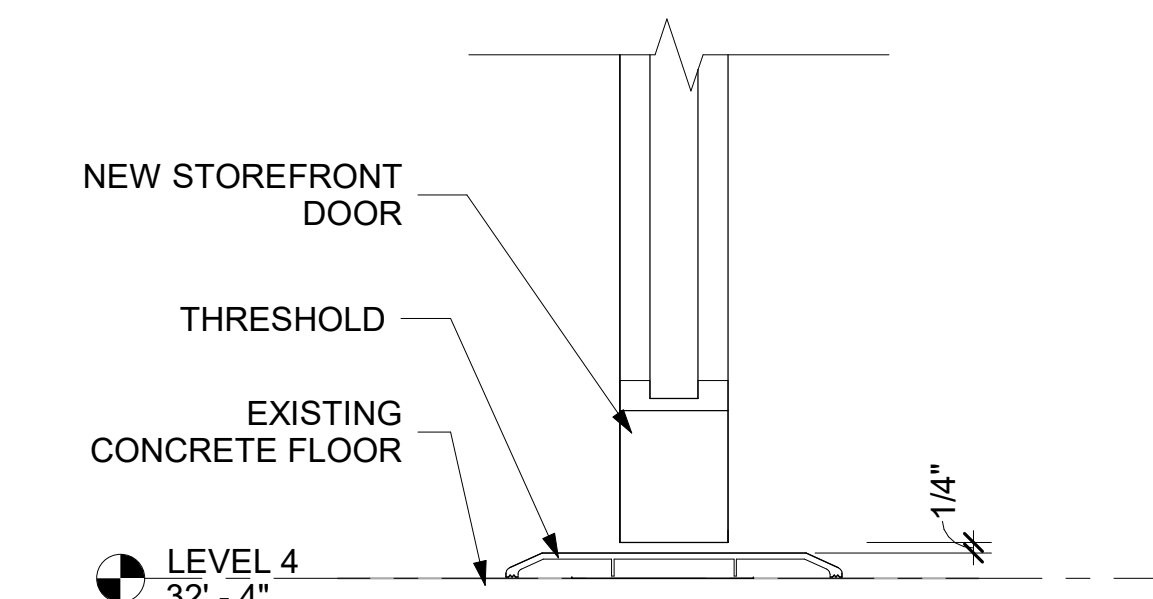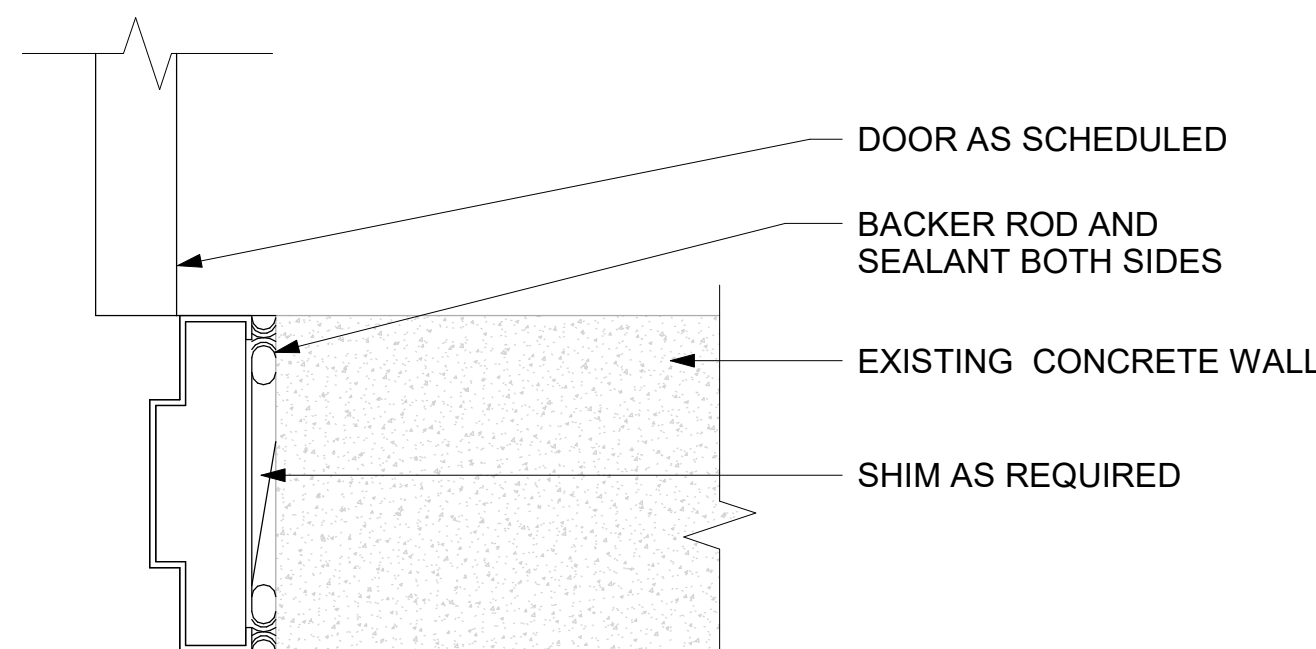


8 DOOR THRESHOLD @ STOREFRONT
3" = 1'-0"

DOOR SCHEDULE													
MARK	ROOM #	ROOM NAME	DOOR SIZE			DOOR TYPE	GLAZING TYPE	HW SET	MATERIAL		FIRE RATING	STC RATING	COMMENTS
			WIDTH	HT	THK				DOOR	FRAME			
401	401	EQUIP	6' - 0"	6' - 8"	0' - 1 3/4"	1B	-	E8	SS	SS	-	-	18" SQ. LOUVER IN DOOR
402	402	ELEV LOBBY	3' - 0"	7' - 0"	0' - 1 3/4"	1A	TEMPERED	E4	GLASS	HM	-	-	

SEE SPECIFICATION 08 71 00 FOR DOOR HARDWARE

LOUVER SCHEDULE		
MARK	WIDTH	HEIGHT
LV-1	3' - 0 1/4"	2' - 7"
LV-2	1' - 0"	2' - 7"
LV-3	3' - 0"	2' - 7"
LV-4	2' - 10 1/2"	2' - 7"

*DOOR HEIGHTS AND WIDTHS PER SCHEDULE

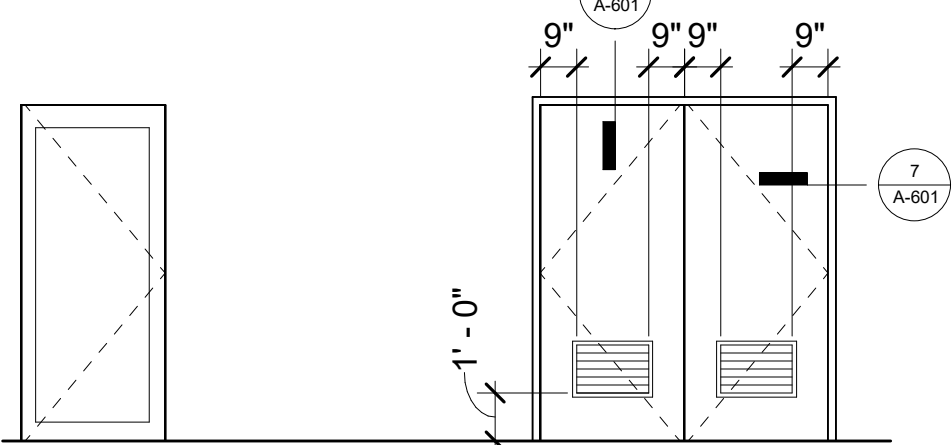


1A 1B


GLAZING TYPES

G-1: COATED SINGLE PANE


G-2: ALUMINUM SPANDREL

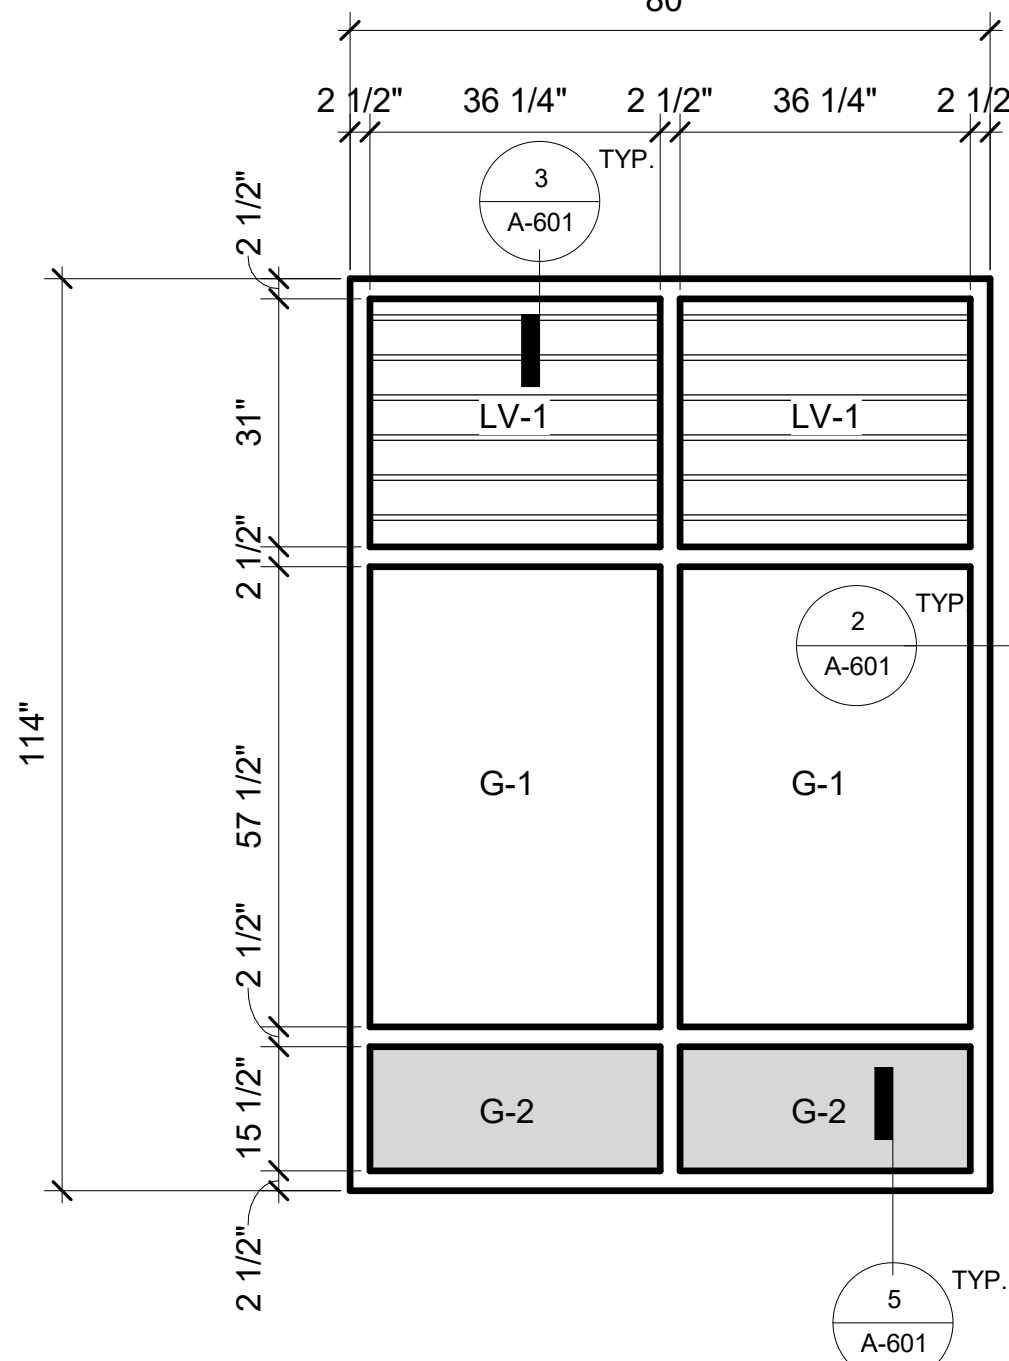

SF-1

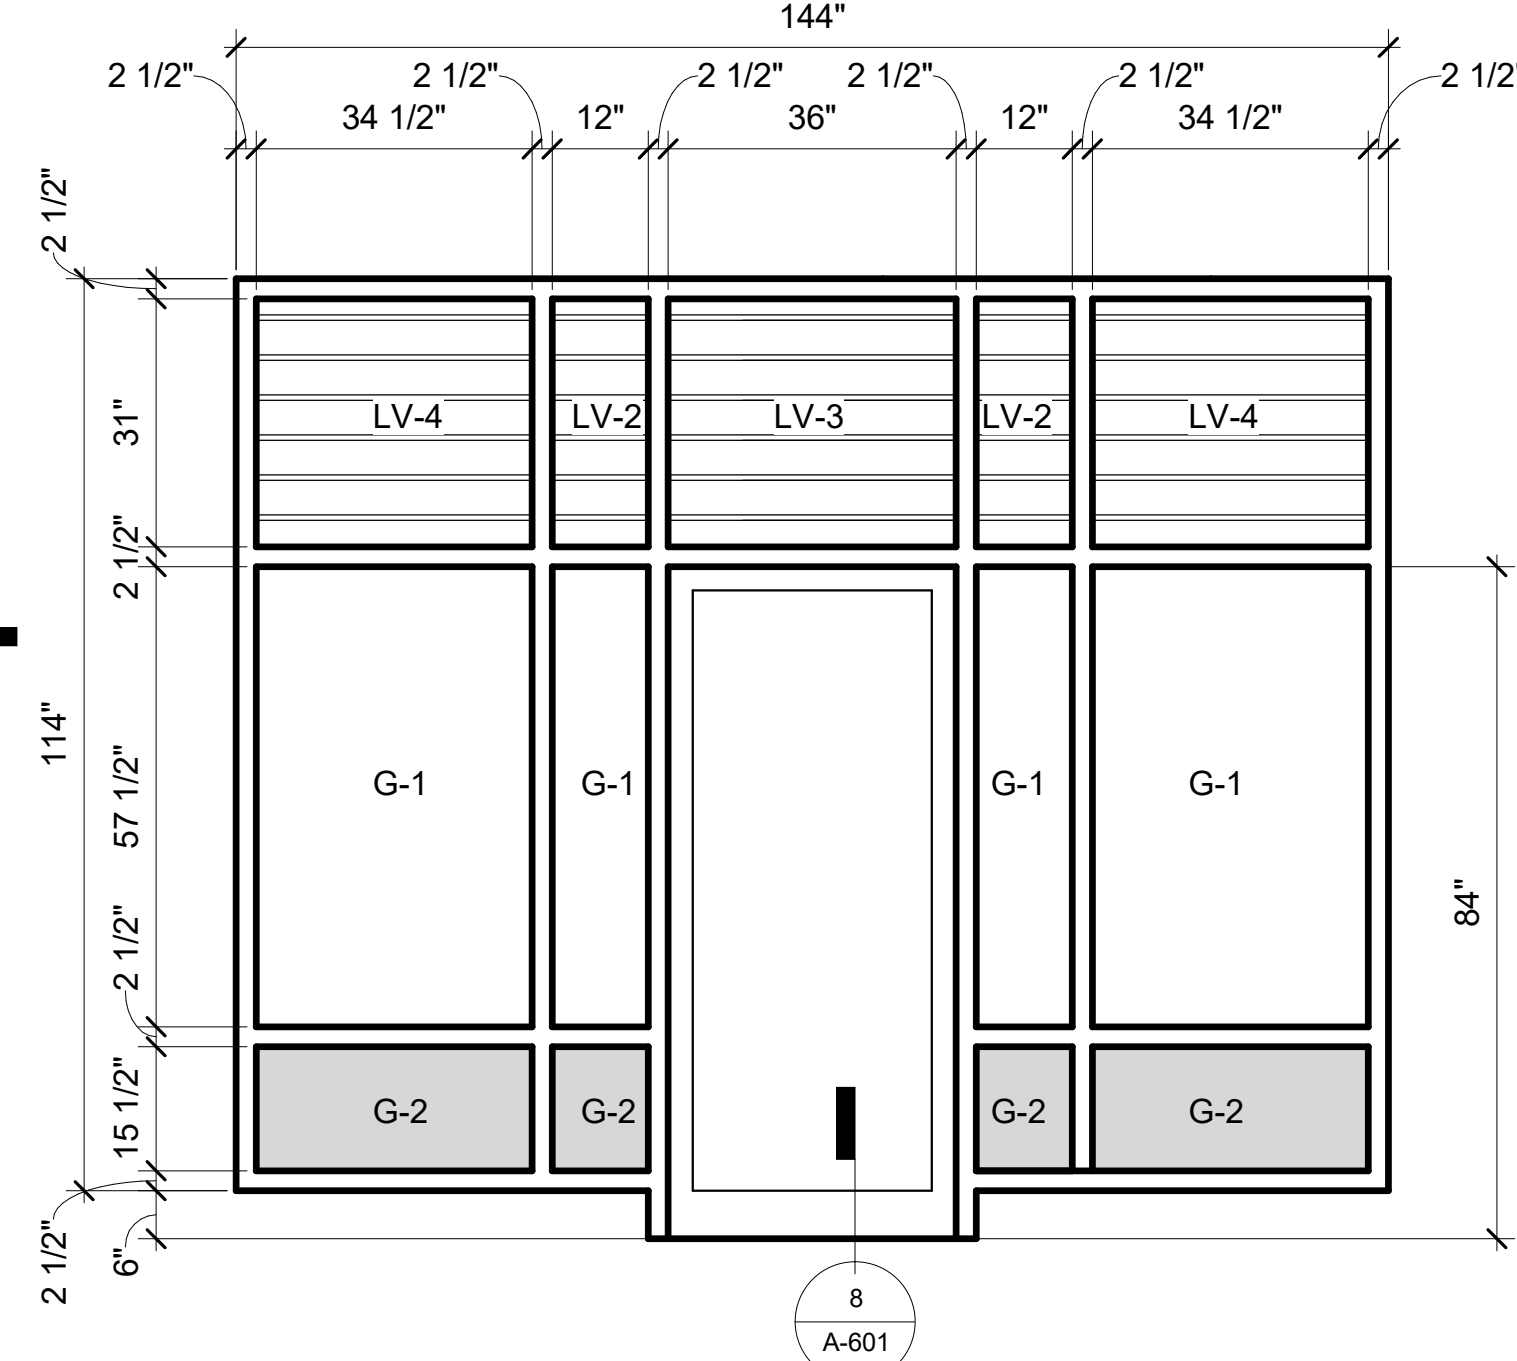

SF-2

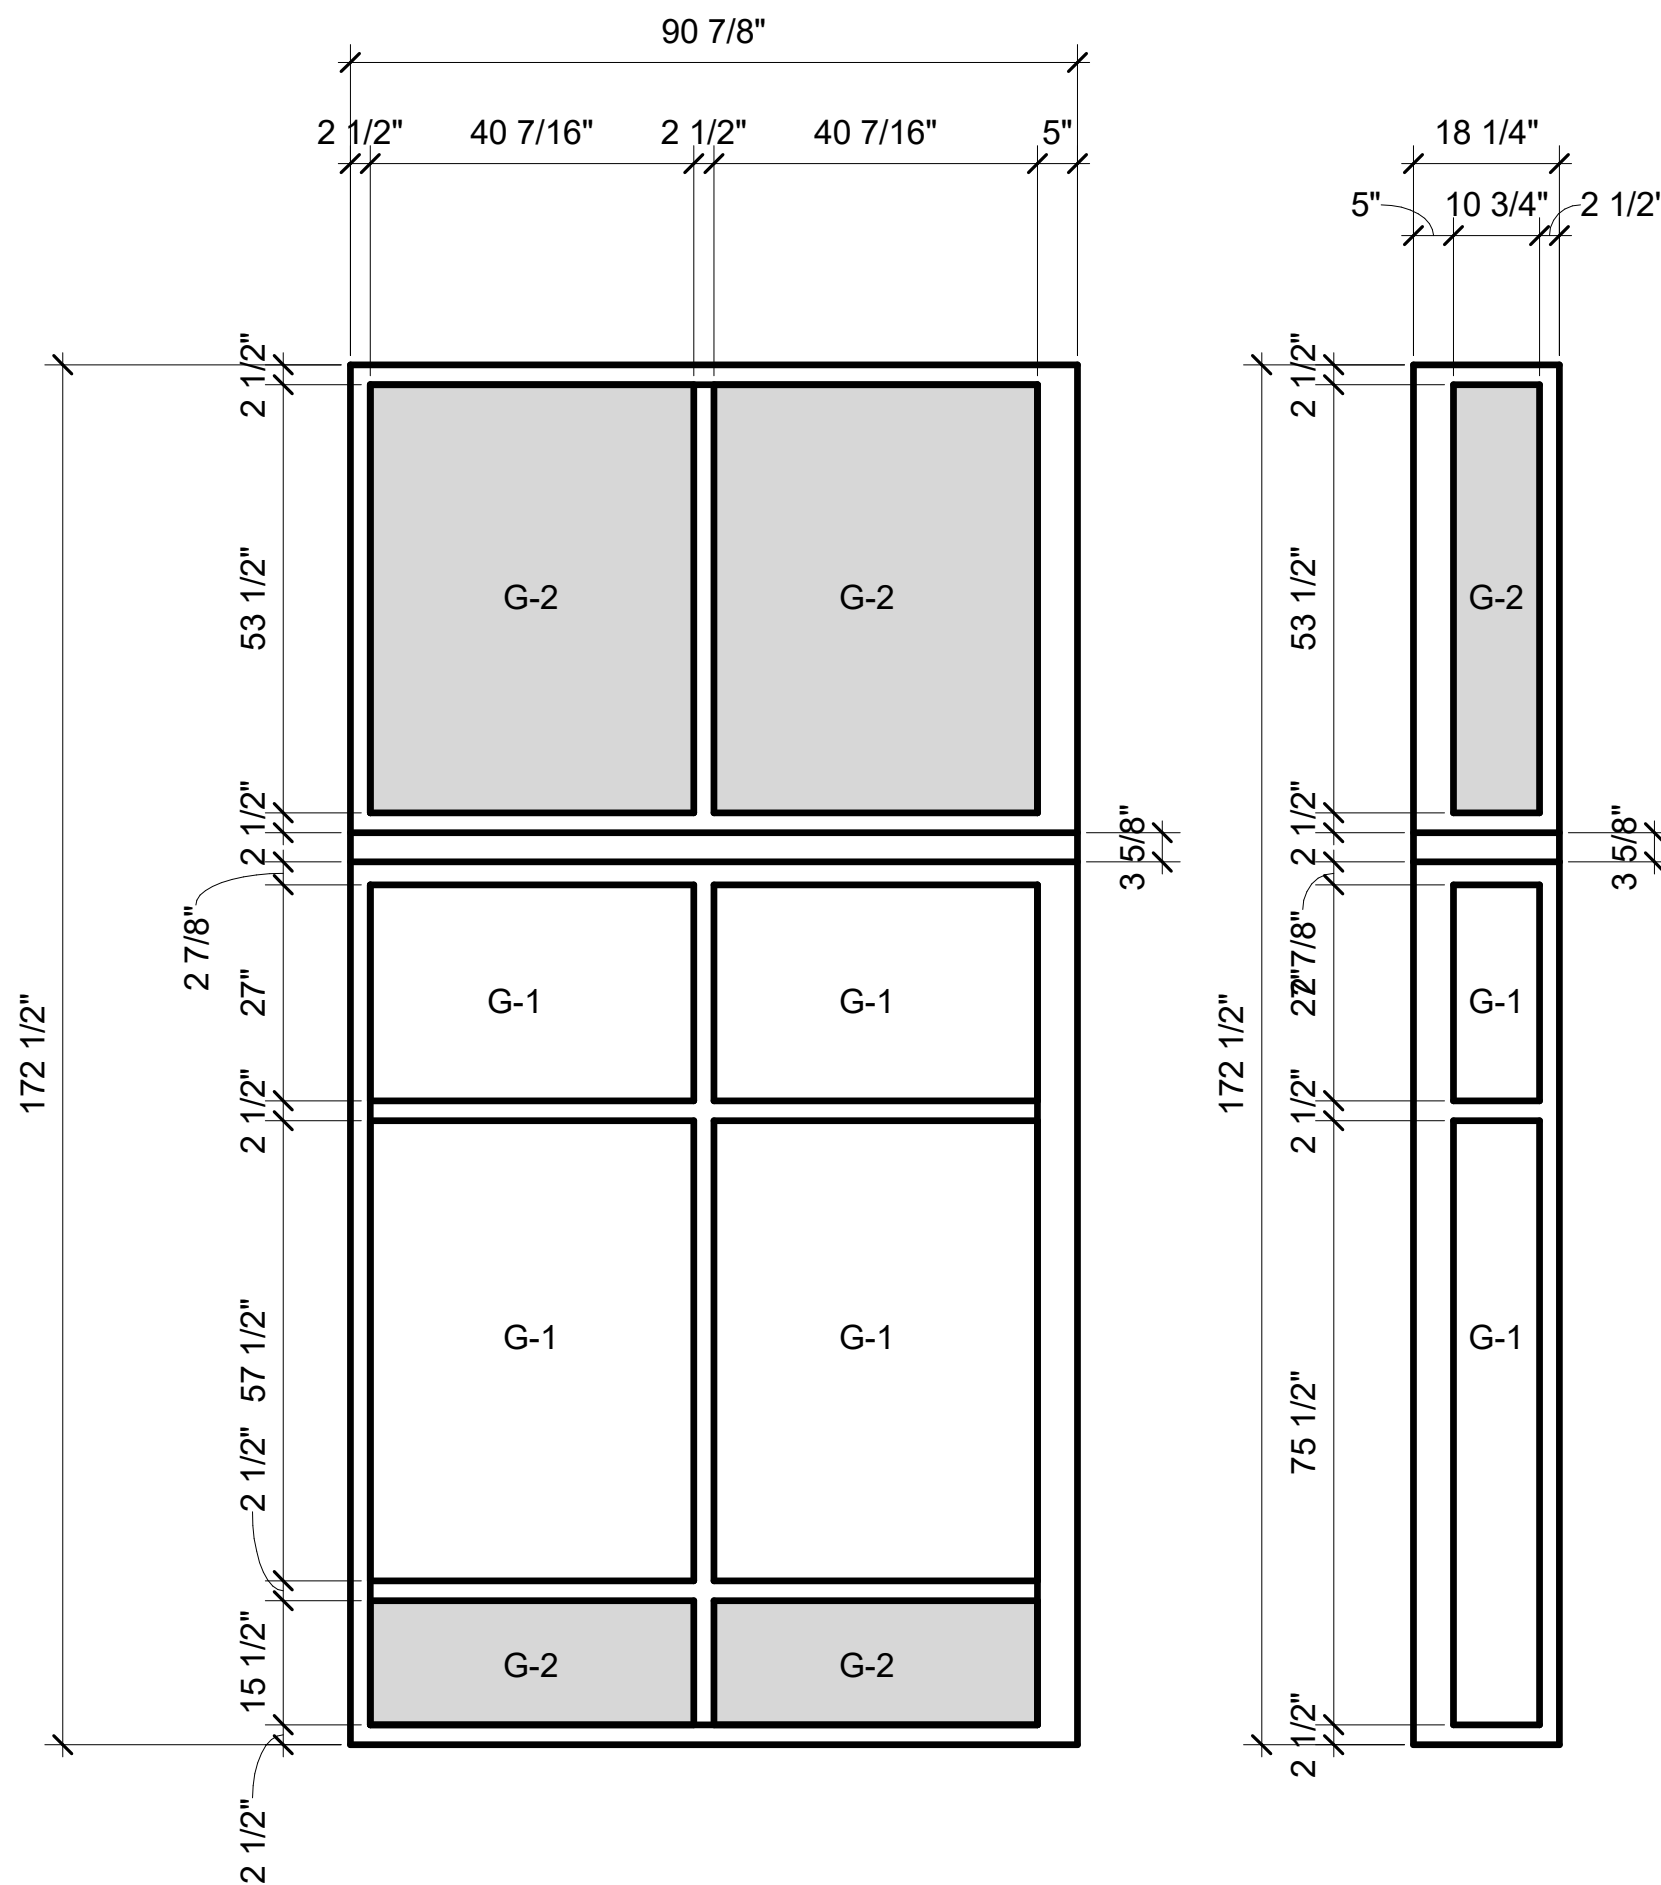

SF-3

SF-4

GENERAL NOTES

- SEE SPECIFICATION SECTION 08 71 00 - DOOR HARDWARE FOR HW SETS.

		CONSULTANT	ARCHITECT/ENGINEER OF RECORD	STAMP	Office of Capital Projects	Drawing Title ELEVATOR SCOPE, DOOR SCHEDULE, TYPES & DETAILS	Phase 100% CONSTRUCTION DOCUMENTS	Project Title REPAIR AND WEATHERIZE PARKING STRUCTURE 211 ELEVATOR	Project Number 662-23-111
		ENGINEERING DISCIPLINE:	A/E: SPEES DESIGN BUILD 23830 PACIFIC HIGHWAY S, SUITE 300 KENT, WA 98032	10000 REGISTERED ARCHITECT JAMES M. KING STATE OF WASHINGTON 11/12/2025	U.S. Department of Veterans Affairs	Approved:		Location SAN FRANCISCO VA MEDICAL CENTER - SAN FRANCISCO, CA	Building Number 211
								Issue Date 11/17/2025	Drawing Number A-601
								Checked MK	
								Drawn AJ	
		Revisions:	Date:						

CODES AND STANDARDS

MATERIAL SPECIFIC STANDARDS ARE LISTED IN THE RESPECTIVE MATERIAL SECTION.

- VA SEISMIC DESIGN REQUIREMENTS, H-16-8, NOVEMBER 1ST 2024
- 2024 INTERNATIONAL BUILDING CODE (IBC) WITH STATE AND LOCAL AMENDMENTS

DESIGN LOADS

REFERENCES:

ASCE 7-22 MINIMUM DESIGN LOADS FOR BUILDINGS AND OTHER STRUCTURES
VA STRUCTURAL DESIGN MANUAL PG-18-10 OCTOBER 1ST 2022, REVISED JULY 1, 2023

DEAD LOADS

WEIGHT OF STRUCTURAL ELEMENTS AND PERMANENT FIXED EQUIPMENT.

SUPERIMPOSED DEAD LOADS

LOCATION	CATEGORY	UNIFORM LOAD (PSF)
ROOF	ROOFING MATERIALS	18

LIVE AND ROOF LIVE LOADS

OCCUPANCY OR USE	UNIFORM LOAD (PSF)	CONCENTRATED LOAD (LBS)
STAIRS & EXITS	100	300
ROOF	20	300
PARKING GARAGE	40	3000 (4.5"x4.5')

SNOW LOAD

DESIGN PARAMETER	VALUE
SNOW LOAD IMPORTANCE FACTOR, Is	1.2
GROUND SNOW LOAD, Pg	6 PSF
SNOW LOAD ON FLAT ROOFS, Pf	20 PSF
EXPOSURE CATEGORY	D
SNOW LOAD EXPOSURE FACTOR, Ce	1.0
THERMAL FACTOR, Ct	1.0

WIND LOAD

REFER TO THE COMPONENTS AND CLADDING DIAGRAMS AT THE END OF THE GENERAL NOTES SECTION.

DESIGN PARAMETER	VALUE
BASIC WIND SPEED (3-SEC GUST), V	103 MPH
WIND EXPOSURE CATEGORY	D
KZT	1.95
ENCLOSURE CLASSIFICATION	ENCLOSED
INTERNAL PRESSURE COEFFICIENT	±0.18

SEISMIC LOAD

DESIGN PARAMETER	VALUE
SEISMIC IMPORTANCE FACTOR, Is	1.5
SITE LOCATION	LATITUDE: 37.762484° N LONGITUDE: -122.506754° E
SOIL SITE CLASS	C
MAPPED SPECTRAL ACCELERATION	SHORT PERIOD, Ss: 2.12 1-SECOND PERIOD, S1: 0.82
DESIGN SPECTRAL ACCELERATION	SHORT PERIOD, Sds: 1.48 1-SECOND PERIOD, Sd1: 0.078
SEISMIC DESIGN CATEGORY	F

GENERAL CONDITIONS

- CONFLICTS BETWEEN THE DRAWINGS AND SPECIFICATIONS MUST BE BROUGHT TO THE ATTENTION OF THE CONTRACTING OFFICER AND STRUCTURAL ENGINEER OF RECORD (SER) IN WRITTEN FORM AND RESOLVED BEFORE PROCEEDING WITH AFFECTED WORK.
- STRUCTURAL DRAWINGS REPRESENT THE COMPLETED STRUCTURE. THE CONTRACTOR IS RESPONSIBLE FOR THE MEANS AND METHODS NECESSARY TO COMPLETE THE WORK, FOR JOB SITE SAFETY AND FOR COORDINATING WITH OTHER DISCIPLINES AS REQUIRED.
- THE CONTRACTOR IS RESPONSIBLE FOR THE ERECTION PROCEDURE AND SEQUENCING TO ENSURE STABILITY OF THE STRUCTURE DURING CONSTRUCTION. PROVIDE SHORING, BRACING, AND FALSEWORK AS NEEDED TO PROTECT THE STRUCTURE THROUGHOUT CONSTRUCTION.
- ERECTION AIDS FOR FACILITATING CONSTRUCTION NOT SHOWN IN THESE DRAWINGS MUST BE REMOVED AND ELEMENTS RESTORED TO ITS ORIGINAL DESIGN INTENT SHOWN PER THESE DRAWINGS.
- STRUCTURAL DRAWINGS SHOW GENERAL AND TYPICAL DETAILS OF CONSTRUCTION. WHERE SPECIFIC CONDITIONS ARE NOT SHOWN, DETAILS OF SIMILAR TYPE AND CHARACTER MAY BE USED BUT REQUIRE APPROVAL FROM THE SER.
- TYPICAL DETAILS MAY NOT BE REFERENCED FROM THE PLANS BUT APPLY FOR THE CONDITIONS AS DESCRIBED BY THE DETAIL.
- CONTRACTOR-INITIATED CHANGES REQUIRE APPROVAL FROM THE SER.
- FOR A CONTRACTOR REQUESTED DESIGN REVISION, THE PROPOSED ALTERNATIVE MUST BE SUBMITTED TO THE CONTRACTING OFFICER FOR REVIEW AND APPROVAL BY THE SER. THE SUBMITTAL MUST INCLUDE DRAWINGS, STRUCTURAL DETAILS AND RELATED CALCULATIONS, STAMPED AND SIGNED BY A PROFESSIONAL ENGINEER LICENSED TO PRACTICE IN THE JURISDICTION OF THE PROJECT LOCATION. CALCULATIONS MUST DEMONSTRATE COMPLIANCE WITH THE CODES AND DESIGN REQUIREMENTS LISTED PER THESE DRAWINGS, AND THAT THE ALTERNATIVE DESIGN DOES NOT ADVERSELY AFFECT THE STRUCTURE SHOWN IN THESE DRAWINGS.
- CONTRACTOR MUST COORDINATE THESE DRAWINGS WITH THE DRAWINGS OF THE OTHER DISCIPLINES AND SPECIFICATIONS FOR ADDITIONAL INFORMATION NOT SHOWN ON THE STRUCTURAL DRAWINGS. EXAMPLES INCLUDE EMBEDDED ANCHORS, SLEEVES AND INSERTS, MISCELLANEOUS ATTACHMENT DETAILS, FLOOR FINISHES, DOOR THRESHOLDS, SLOPES TO DRAINS, OPENINGS IN STRUCTURAL ELEMENTS, ETC.
- VERIFY DIMENSIONS AND DETAILS PRIOR TO FABRICATION AND CONSTRUCTION. THIS INCLUDES COORDINATING THE SIZE AND LOCATION OF OPENINGS THROUGH STRUCTURAL ELEMENTS WITH THE RESPECTIVE SUBCONTRACTOR, AS WELL AS COORDINATING INSERTS AND ATTACHMENTS FOR USE BY OTHER TRADES.
- NO PIPES OR DUCTS MAY BE PLACED IN STRUCTURAL MEMBERS UNLESS DETAILED BY THE STRUCTURAL PLANS OR APPROVED BY THE SER.
- DIMENSIONS MUST NOT BE SCALED FROM THE DRAWINGS.
- PROVIDE SUBMITTALS AND (FABRICATION, AND ERECTION, ETC.) SHOP DRAWINGS FOR THE WORK SHOWN IN THESE DRAWINGS TO THE CONTRACTING OFFICE FOR APPROVAL FROM THE SER. WORK MUST NOT PROCEED WITHOUT REVIEW AND APPROVAL BY THE SER.
- SHOP DRAWINGS MUST BE SUBMITTED TO THE CONTRACTING OFFICER FOR REVIEW AND APPROVAL PRIOR TO FABRICATION. UNLESS NOTED OTHERWISE, PROVIDE SHOP DRAWINGS FOR:
 - DEFORMED BAR REINFORCING LAYOUT FOR CONCRETE AND MASONRY.
 - STRUCTURAL AND MISCELLANEOUS STEEL.
 - INCLUDE LOCATIONS OF EXISTING REINF. WITH SUBMITTAL FOR PLATES WITH ANCHORS INTO EXISTING STRUCTURAL MEMBERS.
- BY SUBMITTING FOR ENGINEER'S REVIEW, THE CONTRACTOR CONFIRMS THE ACCURACY OF THE SUBMITTALS FOR DIMENSIONS, QUANTITIES, ELEMENT SIZES, CONSTRUCTION MATERIALS, FIELD MEASUREMENTS AND THAT THE CONTENTS HAVE BEEN REVIEWED FOR MEANS, METHODS, AND OPERATIONS OF CONSTRUCTION, AND FOR ITS ADHERENCE TO SAFETY PROTOCOLS AT THE SITE.
- SHOP DRAWING REVIEW DOES NOT RELIEVE THE CONTRACTOR FROM HAVING SOLE RESPONSIBILITY FOR THE ACCURACY OF ELEMENT SIZES, DIMENSIONS AND DETAILS. SUCH REVIEW DOES NOT CONSTITUTE ACCEPTANCE BY THE ENGINEER OF THE CORRECTNESS OR ADEQUACY OF SUCH SUBMITTALS. NOR IS A WARRANTY THAT THE SUBMITTALS SATISFY THE REQUIREMENTS OF THE CONTRACT.

CAST IN PLACE CONCRETE

- REFERENCES:
 - ACI 301-20 SPECIFICATIONS FOR CONCRETE CONSTRUCTION
 - ACI 318R-18 DETAILS AND DETAILING CONCRETE CONSTRUCTION
 - ACI 318-19 BUILDING CODE REQUIREMENTS FOR STRUCTURAL CONCRETE
 - ACI 347-14 GUIDE TO FORMWORK FOR CONCRETE
- CONCRETE WORK MUST CONFORM TO ACI 301. FORMWORK MUST CONFORM TO ACI 347.
 - MINIMUM CONCRETE PROPERTIES AT 28-DAYS PER THE FOLLOWING TABLE.

LOCATION	MIN 28-DAY COMPRESSIVE STRENGTH (PSI)	ACI 318, CH. 19 EXPOSURE CATEGORIES						NOMINAL MAX AGGREGATE SIZE
		FREEZING & THAWING	SULFATE	WATER CONTACT	CORROSION PROTECTION	MAX WATER/CEMENT RATIO	CEMENT TYPE	
CONCRETE CURB	4,000	F2	S1	W1	C1	0.45	II	1"
- CONCRETE EXPOSED TO THE ENVIRONMENT MUST HAVE 6% +/- 1% AIR ENTRAINMENT BY VOLUME PER ASTM C260.
- BEFORE CASTING THE SECOND SIDE OF A CONSTRUCTION JOINT, ROUGHEN SURFACE OF CONCRETE ELEMENTS AT CONSTRUCTION JOINTS TO A MINIMUM AMPLITUDE OF 1/4 INCH, UNLESS NOTED OTHERWISE. CLEAN AND APPLY BONDING AGENT TO THE HARDENED CONCRETE SURFACE RECEIVING FRESH CONCRETE.
- SECTIONS AND DETAILS MAY NOT SHOW ALL REQUIRED DEFORMED BAR REINFORCEMENT FOR CLARITY. ADDITIONAL REINFORCEMENT MAY BE DESCRIBED IN PLANS, SCHEDULES, NOTES, OR OTHER DETAILS, AS APPLICABLE.
- COORDINATE FLOOR FINISHES, SLAB SLOPES & DEPRESSIONS, FLOOR DRAINS, CURBS, CONCRETE PADS, AND OTHER CONCRETE FEATURES IDENTIFIED IN THE CONTRACT DOCUMENTS.
- THE STRUCTURAL DRAWINGS DO NOT NECESSARILY SHOW ALL ITEMS EMBEDDED IN THE CONCRETE. COORDINATE AND PROVIDED EMBEDDED ITEMS AS SHOWN IN THE CONTRACT DOCUMENTS AND AS REQUIRED BY THE EQUIPMENT MANUFACTURERS, AS NEEDED.
- NON-STRUCTURAL STEEL MEMBERS EMBEDDED IN CONCRETE MUST BE HOT-DIP GALVANIZED OR PAINTED. DAMAGED COATINGS OF EMBEDDED ITEMS MUST BE REPAIRED PRIOR TO CASTING CONCRETE.
- PENETRATIONS THROUGH CONCRETE WALLS OR SLABS MUST CONFORM TO STANDARD DETAIL DRAWINGS.
- PROVIDE 3/4" CHAMFER ON EXPOSED CONCRETE EDGES UNLESS NOTED OTHERWISE.

REINFORCING STEEL

- REFERENCES:
 - ACI 301-20 SPECIFICATIONS FOR CONCRETE CONSTRUCTION
 - ACI SP-66-04 ACI DETAILING MANUAL
 - ACI 318R-18 DETAILS AND DETAILING CONCRETE CONSTRUCTION
 - AWS D1.4:2018 STRUCTURAL WELDING CODE – REINFORCING STEEL
- STEEL REINFORCEMENT MUST CONFORM TO:

CONDITION	STANDARD AND GRADE	MIN YIELD (KSI)
TYPICAL DEFORMED BAR	ASTM A615 GR 60 OR ASTM A706	60
- PROVIDE BAR SUPPORTS AND SPACERS PER ACI 315 UNLESS NOTED OTHERWISE. DEFORMED BAR REINFORCEMENT AND INSERTS MUST BE SECURED IN-PLACE PRIOR TO PLACING CONCRETE. DO NOT PLACE REBAR MATS DIRECTLY AGAINST SOIL. REBAR MATS ADJACENT TO SOIL OR OVER MUD SLABS MUST BE SUPPORTED BY CHAIRS, DO NOT LIFT INTO PLACE DURING POURING.
- UNLESS INDICATED OTHERWISE, REINFORCEMENT BARS ARE CONTINUOUS AND MUST BE LAP SPLICED OR COUPLED WITH MECHANICAL CONNECTORS. LAP LENGTH NOTES:
 - SEE DEVELOPMENT AND LAP SPLICE LENGTH SCHEDULES FOR REINFORCEMENT DETAILS.
 - LAP SPLICE LENGTH MUST BE USED FOR THE LARGER BAR SIZE WHEN BAR SIZE TRANSITIONS AT LAP.
 - OVERLAP WELDED WIRE LAYER REINFORCEMENT A LENGTH OF 1.5X WIRE DEVELOPMENT LENGTH OR ONE CROSSWIRE SPACING PLUS 2 INCHES, WHICHEVER IS LARGER.
 - MECHANICAL CONNECTORS MUST HAVE A MINIMUM CAPACITY OF 1.25 X YIELD STRENGTH OF THE BAR.
 - MECHANICAL CONNECTORS IN MEMBERS DESIGNATED AS PART OF THE SEISMIC-FORCE-RESISTING SYSTEM MUST HAVE A MINIMUM CAPACITY EQUAL TO THE TENSILE STRENGTH OF THE BAR.
- TYPE 1 MECHANICAL CONNECTORS MUST DEVELOP 126% OF THE YIELD STRENGTH (Fy) OF THE STRONGER OF THE TWO BARS BEING SPLICED. TYPE 2 MECHANICAL CONNECTORS MUST DEVELOP THE FULL TENSILE STRENGTH OF THE STRONGER OF THE TWO BARS BEING SPLICED, WHERE MECHANICAL CONNECTORS ARE USED IN LIEU OF LAP SPLICES. PROVIDE TYPE 2 MECHANICAL CONNECTORS EXCEPT WHERE TYPE 1 ARE PERMITTED AS INDICATED.
- HEADED DEFORMED BARS (TERMINATORS) MUST BE INTEGRALLY FORMED OR THREADED DEVICES MEETING THE REQUIREMENTS OF ACI 318, SECTION 25.4.4.1.
- UNLESS NOTED OTHERWISE ON THE DRAWINGS:
 - DEFORMED BAR COVER MUST CONFORM TO SPECIFIED CONCRETE COVER REQUIREMENTS OF ACI 318.
 - REINFORCEMENT MUST BE CONTINUOUS THROUGH CONSTRUCTION JOINTS.
 - APPROVAL FROM SER REQUIRED BEFORE WELDING NON-ASTM A706 Gr. 60 REINFORCEMENT.
 - APPROVAL FROM SER REQUIRED BEFORE FIELD BENDING REINFORCEMENT PARTIALLY EMBEDDED CONCRETE.
 - MATCH DOWELS TO THE LARGER OF MULTIPLE BAR SIZES.
- DOWELS MUST BE SECURED WITH A RIGID TEMPLATE TO ENSURE SPLICE IS LOCATED INSIDE THE CONFINED REGION (REGION ENCLOSED BY SHEAR OR HORIZONTAL REINFORCEMENT) OF CROSS-SECTION.

STRUCTURAL STEEL

- REFERENCES:
 - AISC 303-22 CODE OF STANDARD PRACTICE FOR STEEL BUILDINGS AND BRIDGES.
 - AISC 360-16 SPECIFICATION FOR STRUCTURAL STEEL BUILDINGS.
 - ACI 341-16 SEISMIC PROVISIONS FOR STEEL BUILDINGS.
 - AISC RESEARCH COUNCIL ON STRUCTURAL CONNECTIONS (RCSC) SPECIFICATION FOR STRUCTURAL JOINTS USING HIGH-STRENGTH BOLTS 2014.
- STRUCTURAL STEEL WORK MUST BE PERFORMED BY AISC CERTIFIED FABRICATORS & ERECTORS.
- STEEL CONSTRUCTION AND DESIGN AS PART A DEFERRED DESIGN SUBMITTAL MUST CONFORM TO AISC 360 AND AISC 303.
- USE STRUCTURAL STEEL SHAPES (AS APPLICABLE PER THE DRAWINGS), WITH CROSS-SECTIONS PER ASTM A6, PER THE FOLLOWING TABLE.

SHAPE	STANDARD & GRADE (UNO)	MIN YIELD (KSI)
WIDE FLANGES (W) AND TEES (WT)	ASTM A992	50
CHANNELS (C & MC) AND ANGLES (L)	ASTM A36	36
PLATE AND FLAT BAR STOCK (PL)	ASTM A36 GR 36	36
HSS RECTANGULAR OR SQUARE ROUND	ASTM A500 GR C ASTM A500 GR C	50 50
PIPE	ASTM A53 GR B	35
OTHER STEEL	ASTM A572	50

- PROVIDE PROTECTIVE COATING AT STEEL EXPOSED TO THE ENVIRONMENT. UNO ALL STEEL TO BE HOT DIPPED GALVANIZED.
- MACHINE COLUMN ENDS AT SPLICES TO PROVIDE A FLUSH BEARING CONTACT SURFACE, UNLESS NOTED OTHERWISE.
- CAMBER MUST BE COLD FORMED PER AISC SPECIFICATIONS AND TOLERANCES.
- USE HIGH STRENGTH (HS) BOLTS PER ASTM F3125, GRADES AS INDICATED IN THE FOLLOWING TABLE, UNLESS NOTED OTHERWISE.

TYPICAL HIGH STRENGTH BOLTS	STANDARD, GRADE, AND NOTES
BOLT DIAMETER BOLT ASTM F3125 GRADE BOLT FINISH/COATING	7/8 INCH DIAMETER, UNO A325, TYPE 1 UNO ASTM F2329 HDG
HEAVY HEX NUT HARDENED WASHER (CIRCULAR, BEVELED OR CLIPPED, AS REQ'D)	ASTM A563 TYPE DH ASTM F436 TYPE 1
DIRECT TENSION INDICATING WASHERS BOLT DIAM. 1-1/2 IN AND SMALLER BOLT DIAM. UP TO 2-1/2 INCHES	ASTM F959 ASTM F2437
TENSION CONTROLLED BOLTS (USE MANUFACTURER SUPPLIED NUTS AND WASHERS)	F1852, TYPE 1

- SLIP-CRITICAL (SC) BOLTS MUST BE PER THE RCSC SPECIFICATION AND INSPECTED IN ACCORDANCE WITH THE IBC.
- USE SNUG-TIGHT (ST) BOLTS PER THE RCSC WHEN SLIP-CRITICAL IS NOT IDENTIFIED IN THE DRAWINGS.
- USE ASTM A449 BOLTS WITH ASTM F563 NUTS AND ASTM F436 HARDENED WASHERS FOR THROUGH BOLTING HSS SHAPES. BOLTS MUST BE SNUG TIGHT ONLY. PROVIDE JAMB NUT TIGHTENED AGAINST STANDARD NUT TO FASTEN CONNECTOR.
- DIRECT TENSION INDICATING (DTI) WASHERS, IF USED FOR HIGH STRENGTH BOLTS, MUST NOT BE TIGHTENED TO A FULLY CRUSHED CONDITION. DTI MUST HAVE THE MINIMUM ACCEPTABLE NUMBER OF TAPERED GAGE REJECTIONS BETWEEN LUGS. REJECTION OF GAGE AT EACH LUG LOCATION IS CAUSE FOR REJECTION OF BOLT INSTALLATION.
- CONTRACTOR MUST SUBMIT A BOLTING PROCEDURE PLAN TO THE CONTRACTING OFFICER FOR REVIEW AND APPROVAL BY THE SER BEFORE BEGINNING WORK.
- BOLT HOLES CUT IN THE FIELD MUST BE DRILLED, NOT BURNED. BOLT HOLES CUT IN THE SHOP MAY BE DRILLED, WATER-JET OR LASER CUT. PLASMA CUTTING HOLES NOT PERMITTED.
- LOCATION OF EMBEDDED ELEMENTS MUST BE COORDINATED WITH CONTRACT DOCUMENTS.
- STEEL COMPONENTS EMBEDDED IN CONCRETE OR MASONRY AT EXTERIOR LOCATIONS, EXPOSED TO EARTH, OR LOCATED IN UNCONDITIONED SPACE, MUST BE HOT-DIPPED GALVANIZED PER ASTM A123.
- AT INTERIOR CONDITIONS (NOT EXPOSED TO WEATHER) AND COMPONENTS EMBEDDED IN CONCRETE OR MASONRY MUST BE LEFT UNPAINTED.
- ERECTION AIDS, WHICH ARE THE SOLE RESPONSIBILITY OF THE CONTRACTOR, MUST BE REMOVED AND THE AFFECTED ELEMENTS RESTORED TO ORIGINAL DESIGN INTENT. ERECTION AIDS AND OTHER ATTACHMENTS ARE NOT PERMITTED IN PROTECTED SEISMIC ZONES OF ELEMENTS WITHOUT PRIOR APPROVAL FROM THE SER.
- NOTIFY CONTRACTING OFFICER OF ANY FABRICATION OR ERECTION ERRORS, OR DEVIATIONS. WRITTEN APPROVAL IS REQUIRED BEFORE FIELD CORRECTIONS ARE MADE.

STRUCTURAL WELDING

- REFERENCES:
 - AWS D1.1:18 STRUCTURAL WELDING CODE – STEEL
- WELDING MUST BE DONE BY AWS CERTIFIED WELDERS AND PER AWS D1.1.
- USE LOW HYDROGEN E70XX ELECTRODE WITH TENSILE STRENGTH PER AWS D1.1, UNLESS NOTED OTHERWISE.
- WELDS THAT ARE PART OF THE SEISMIC FORCE-RESISTING SYSTEM MUST HAVE A MINIMUM CHERRY V-NOTCH TOUGHNESS OF 20 FOOT-POUNDS AT 0° F.
- FIELD WELDING SYMBOLS HAVE NOT NECESSARILY BEEN USED IN THE DRAWINGS. CONTRACTOR MUST COORDINATE THE USE OF SHOP AND FIELD WELDS AS NECESSARY. REPAIR ANY DAMAGED GALVANIZED COATINGS PER ASTM A123.
- FILLET WELD SIZES SHOWN ON DRAWINGS INDICATE THE MINIMUM LEG SIZE REQUIRED AT THE JOINT. INCREASE WELD SIZE BY ROOT GAP DIMENSION IF A GAP EXISTS AT THE JOINT. IF THE INCLUDED ANGLE OF THE TWO CONNECTED PLATES EXCEEDS 90°, THE WELD MUST BE CONTOURED TO PROVIDE AN EFFECTIVE THROAT DIMENSION NO LESS THAN 72% OF WELD SIZE INDICATED. IF NOT SHOWN THE MINIMUM FILLET WELD SIZE AT INTERIOR LOCATIONS MUST BE NO LESS THAN 3/16 INCHES, AND NO LESS THAN 1/4 INCHES AT EXTERIOR LOCATIONS.
- PARTIAL JOINT PENETRATION (PJP) GROOVE WELDS SHOWN ON THE DRAWINGS REFER TO EFFECTIVE THROAT THICKNESS AND MUST BE SIZED ACCORDINGLY FOR THE WELD PROCESS USED.
- COMPLETE JOINT PENETRATION (CJP) MUST HAVE A BACKUP BAR WITH RUNOFF TABS TO ACHIEVE FULL DEPTH OVER FULL LENGTH OF WELD. BACKGROUING THE ROOT IS REQUIRED. BACKUP BAR MUST BE REMOVED AND GROUND SMOOTH, UNLESS NOTED OTHERWISE.
- ULTRASONICALLY TEST (UT) CJP WELDS UPON COMPLETION OF THE WELDED JOINT. PLATE THICKNESS OF 9/16-INCH OR LESS MAY USE MAGNETIC PARTICLE INSPECTION (MPI) OR EDDIE CURRENT ARRAY (ECA) TESTING.
- QUALIFICATIONS AND WELDING PROCEDURE SPECIFICATION (WPS) PER AWS D1.1 AND D1.8 MUST BE SUBMITTED TO THE ENGINEER FOR REVIEW BEFORE STARTING FABRICATION OR ERECTION. COPIES OF THE WPS MUST BE ON SITE AND AVAILABLE TO WELDERS AND THE SPECIAL INSPECTOR.

POST INSTALLED ANCHOR IN CONCRETE AND MASONRY

- EXCEPT WHERE INDICATED ON THE DRAWINGS, POST-INSTALLED ANCHORS CONSIST OF THE FOLLOWING ANCHOR TYPES OR APPROVED EQUAL:

CONDITION	TYPE	ACCEPTABLE ANCHORS
CONCRETE	SCREW	HILTI KWIK HUS-EZ SCREW ANCHORS PER ICC ESR-3027 SIMPSON TITEN HD SCREW ANCHOR PER ICC ESR-2713 DEWALT WEDGE-BOLT+ PER ICC ESR-2526
	EXPANSION	HILTI KWIK-BOLT T2Z ANCHOR PER ICC ESR-4366 SIMPSON STRONG BOLT 2 ANCHOR PER ICC ESR-3037 DEWALT POWER-STUD+ SD1 ANCHOR PER ICC ESR-2818
	ADHESIVE	HILTI HIT-HY 200 ADHESIVE ANCHOR SYSTEM PER ICC ESR-3187 SIMPSON SET-XP ADHESIVE ANCHOR SYSTEM PER ICC ESR-2508 DEWALT PE1000+ ADHESIVE ANCHOR SYSTEM PER ICC ESR-2583
SOLID-GROUTED MASONRY	UNDERCUT	HILTI HD-A-P ADHESIVE ANCHOR PER ICC ESR-1546 SIMPSON TORQ-OUT SELF-UNDERCUTTING ANCHOR PER ICC ESR-2705 DEWALT CCU+ UNDERCUT ANCHOR CARBON STEEL PER ICC ESR-4810
	SCREWS	HILTI KWIK HUS-EZ SCREW ANCHORS PER ICC ESR-3056 SIMPSON TITEN HD SCREW ANCHOR PER ICC ESR-2713 DEWALT SCREW-BOLT+ PER ICC ESR-4042
	EXPANSION	HILTI KWIK-BOLT 3 ANCHOR PER ICC ESR-1385 SIMPSON STRONG BOLT 2 ANCHOR PER ICC ESR-3037 DEWALT POWER-STUD+ SD1 ANCHOR PER ICC ESR-2866
	ADHESIVE	HILTI HIT-HY 270 ADHESIVE SYSTEM PER ICC ESR-4143 SIMPSON SET-XP ADHESIVE SYSTEM PER ICC ESR-2508 DEWALT AC100+GOLD ADHESIVE SYSTEM PER ICC ESR-3200 (STEEL ANCHOR MUST BE ASTM F1554 GRADE 55 CONTINUOUSLY THREADED ROD PER DRAWINGS)

- ANCHOR CAPACITY USED IN DESIGN MUST BE BASED ON THE TECHNICAL DATA PUBLISHED IN THE ICC APPROVAL REPORT. SUBSTITUTION REQUESTS MUST INCLUDE ICC ESR REPORT SHOWING COMPLIANCE WITH RELEVANT BUILDING CODE AND INSTALLATION CATEGORY AND BE APPROVED IN WRITING BY THE CONTRACTING OFFICER FOR REVIEW AND APPROVAL BY THE SER PRIOR TO USE.
- INSTALL ANCHORS PER THE MANUFACTURER INSTRUCTIONS, AS INCLUDED IN THE ANCHOR PACKAGING.
- INSTALL ANCHORS IN ACCORDANCE WITH SPACING AND EDGE CLEARANCES INDICATED ON THE DRAWINGS.
- EXISTING DEFORMED BAR REINFORCEMENT IN THE STRUCTURE MAY CONFLICT WITH SPECIFIC ANCHOR LOCATIONS. UNLESS NOTED OTHERWISE, THE CONTRACTOR MUST LOCATE THE POSITION OF THE EXISTING REINFORCING BARS AND AVOID CUTTING.
- DRILLING, CORING, SAW-CUTTING, ETC. INTO CONCRETE SHALL MEET THE LATEST OSHA REGULATIONS FOR SILICA DUST EXPOSURE.
- ALL ANCHORS SHALL BE HOT-DIPPED GALVANIZED, UNO.

SPECIAL INSPECTION AND TESTING

- SPECIAL INSPECTION AND TESTING MUST CONFORM TO SECTION 1704 OF THE INTERNATIONAL BUILDING CODE (IBC) AS AMENDED BY H-18-8.
- ONE OR MORE QUALIFIED SPECIAL INSPECTION & TESTING AGENCIES MUST BE EMPLOYED TO PERFORM THE NECESSARY INSPECTION OF IBC SECTION 1705, AS APPLICABLE. QUALIFICATIONS FOR SPECIAL INSPECTION AND TESTING AGENCIES AND INSPECTORS MUST BE SUBMITTED TO THE CONTRACTING OFFICER FOR REVIEW AND APPROVAL.
- SPECIAL INSPECTOR QUALIFICATIONS MUST MEET THE REQUIREMENTS OF SPECIFICATION SECTION 01 45 35.
 - FOR STATEMENT OF SPECIAL INSPECTION SEE PROJECT SPECIFICATIONS.
- REPORTING ON SPECIAL INSPECTION AND TESTING MUST CONFORM TO IBC SECTION 1704.5 AND BE SUBMITTED TO THE CONTRACTING OFFICER WEEKLY, OR AS REQUIRED BY THE SPECIFICATIONS.

STRUCTURAL OBSERVATIONS

- STRUCTURAL OBSERVATIONS MUST BE PERFORMED BY THE DESIGNATED REPRESENTATIVE BY THE GOVERNMENT, FOR THE FOLLOWING:
 - STRUCTURAL STEEL: BEAMS AND POST.
 - ANCHORAGE: POST INSTALLED ANCHORS.
- CONTRACTOR MUST NOTIFY CONTRACTING OFFICER 14 DAYS IN ADVANCE OF WHEN WORK IS EXPECTED TO COORDINATE THE DATE OF OBSERVATION.
- STRUCTURAL OBSERVATION DOES NOT WAIVE THE RESPONSIBILITY OF SPECIAL INSPECTION REQUIREMENTS.

Revisions:	Date:

CONSULTANT

ENGINEERING DISCIPLINE:



WSP USA Inc.
1201 Pacific Ave
Suite 550
Tacoma, WA 98402
TEL: (206) 431-2300
FAX: (206) 431-2250


ARCHITECT/ENGINEER OF RECORD

A/E:



SPEEDS DESIGN BUILD
625 1ST AVE, STE 301
SEATTLE, WA 98104
(206) 590-2118
RAY SPEEDS

STAMP

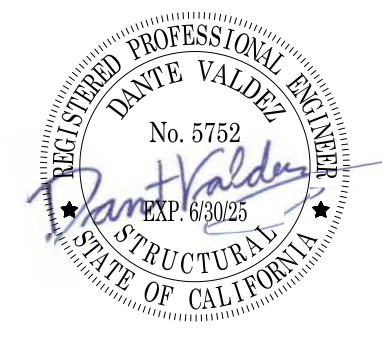

Office of
Capital Projects

 U.S. Department
of Veterans Affairs

Drawing Title

STRUCTURAL GENERAL NOTES

Approved:

Phase

100% CONSTRUCTION
DOCUMENTS (CD)

Project Title

REPAIR AND WEATHERIZE
PARKING STRUCTURE 211
ELEVATOR

Location

SAN FRANCISCO VA MEDICAL CENTER - SAN
FRANCISCO, CA

Issue Date

11/17/2025

Checked

NRT

Drawn

JKM

Project Number

662-23-111

Building Number

211

Drawing Number

S-001

[illegible]

A

B

C

D

E

F

A



B

C

D

E

F



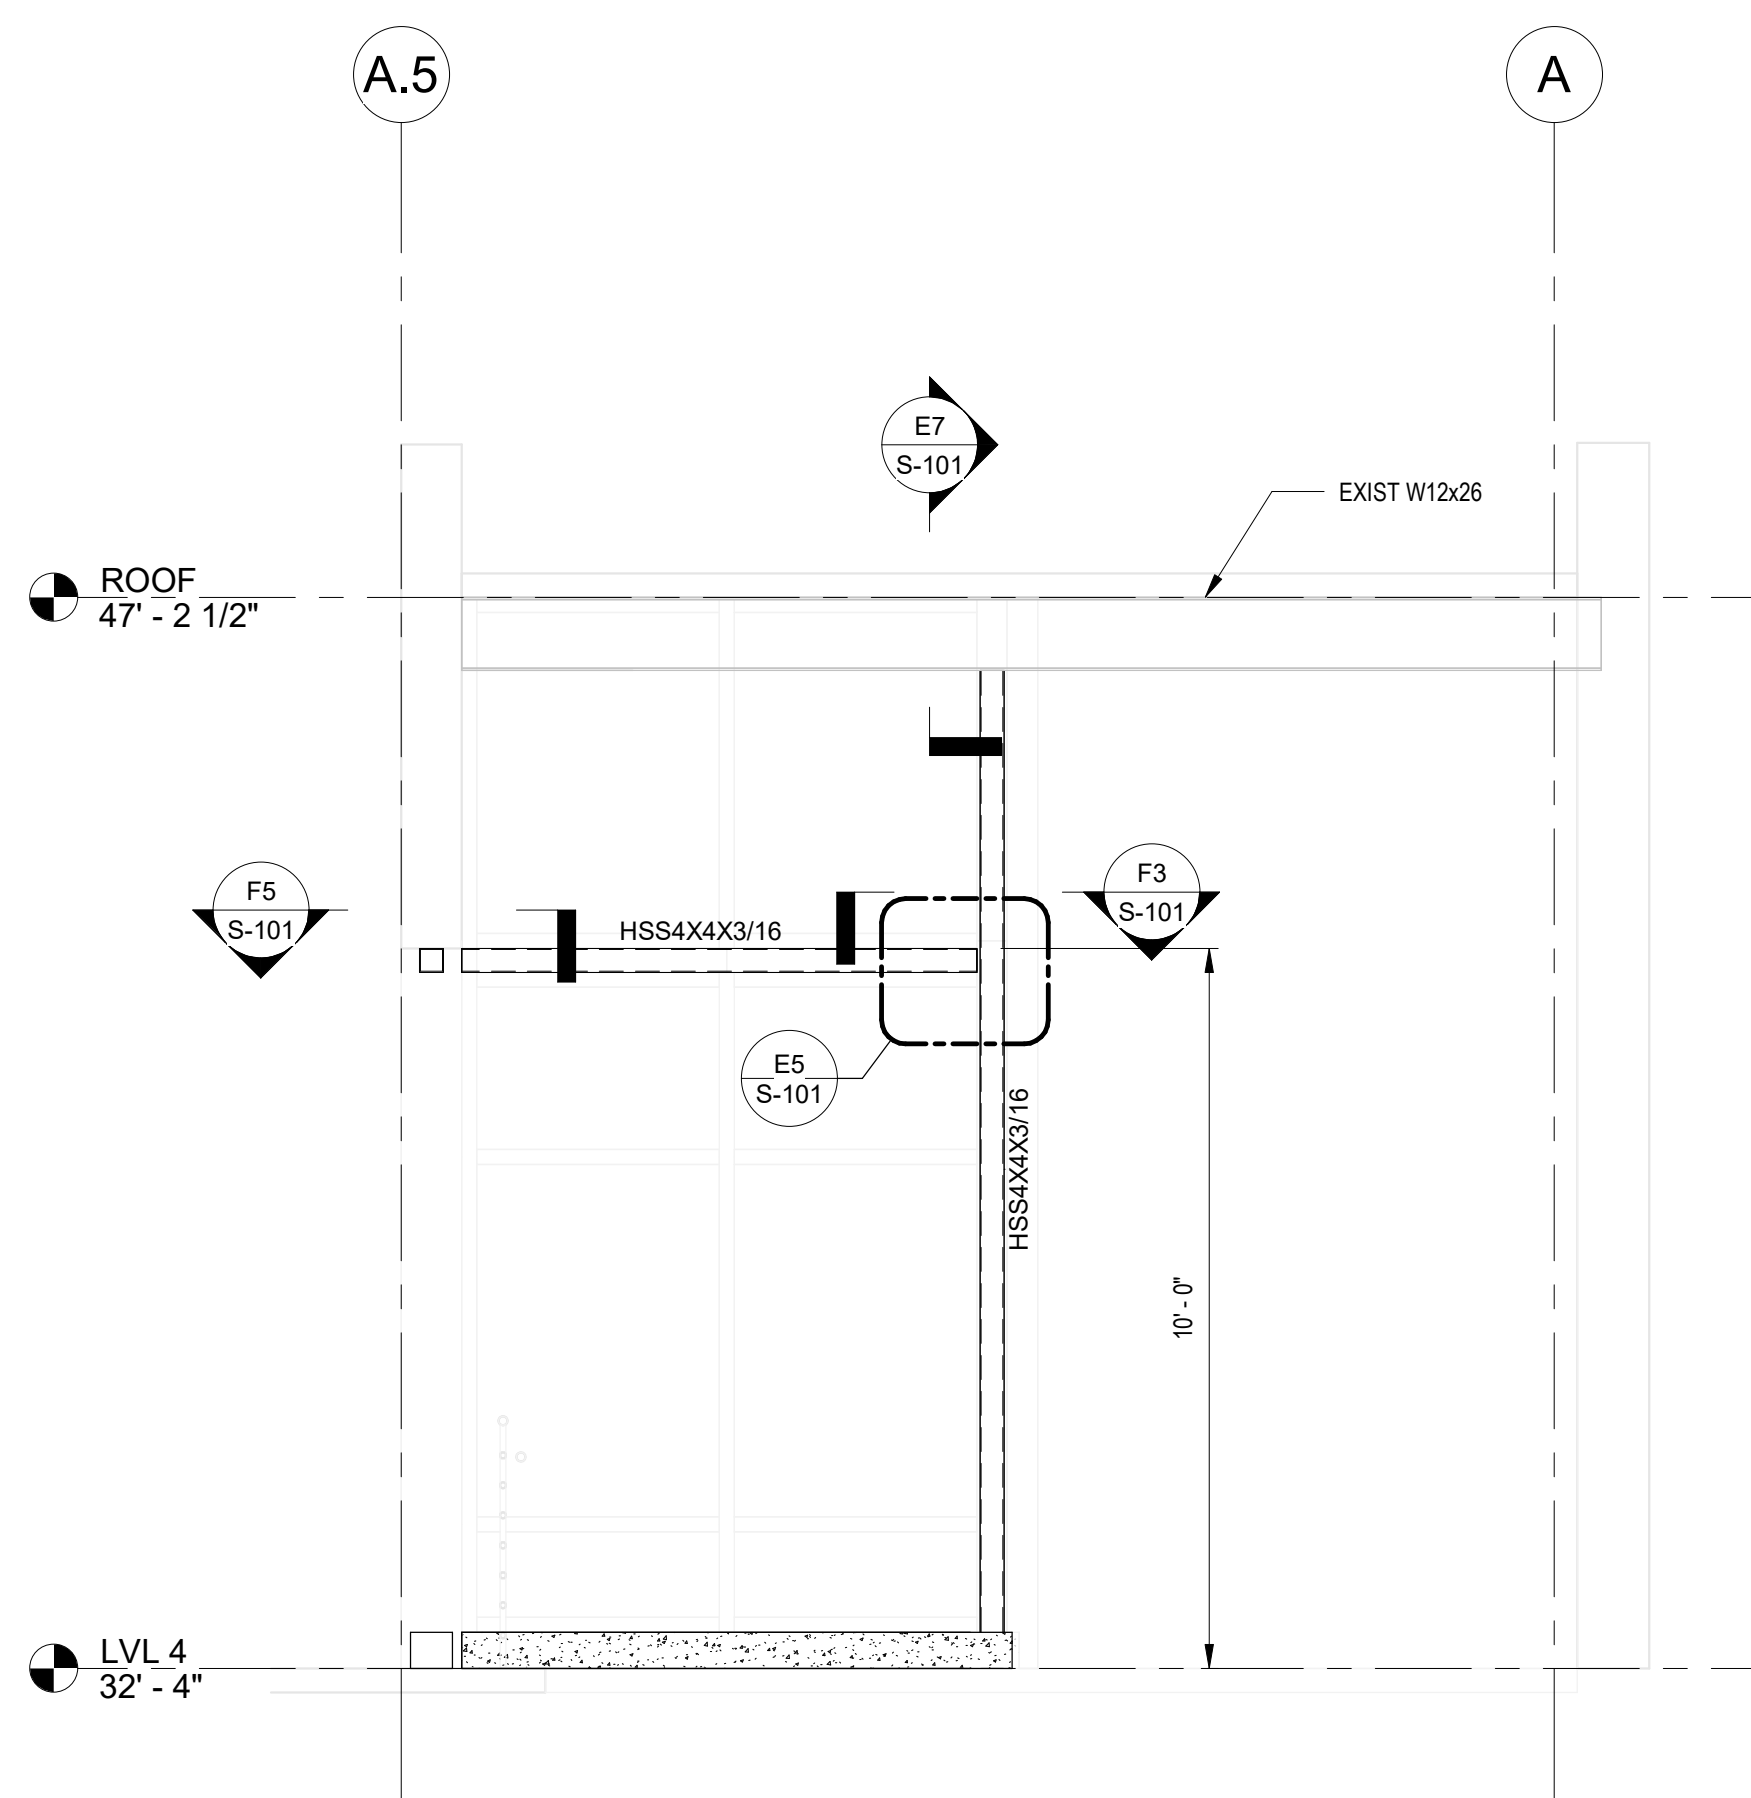
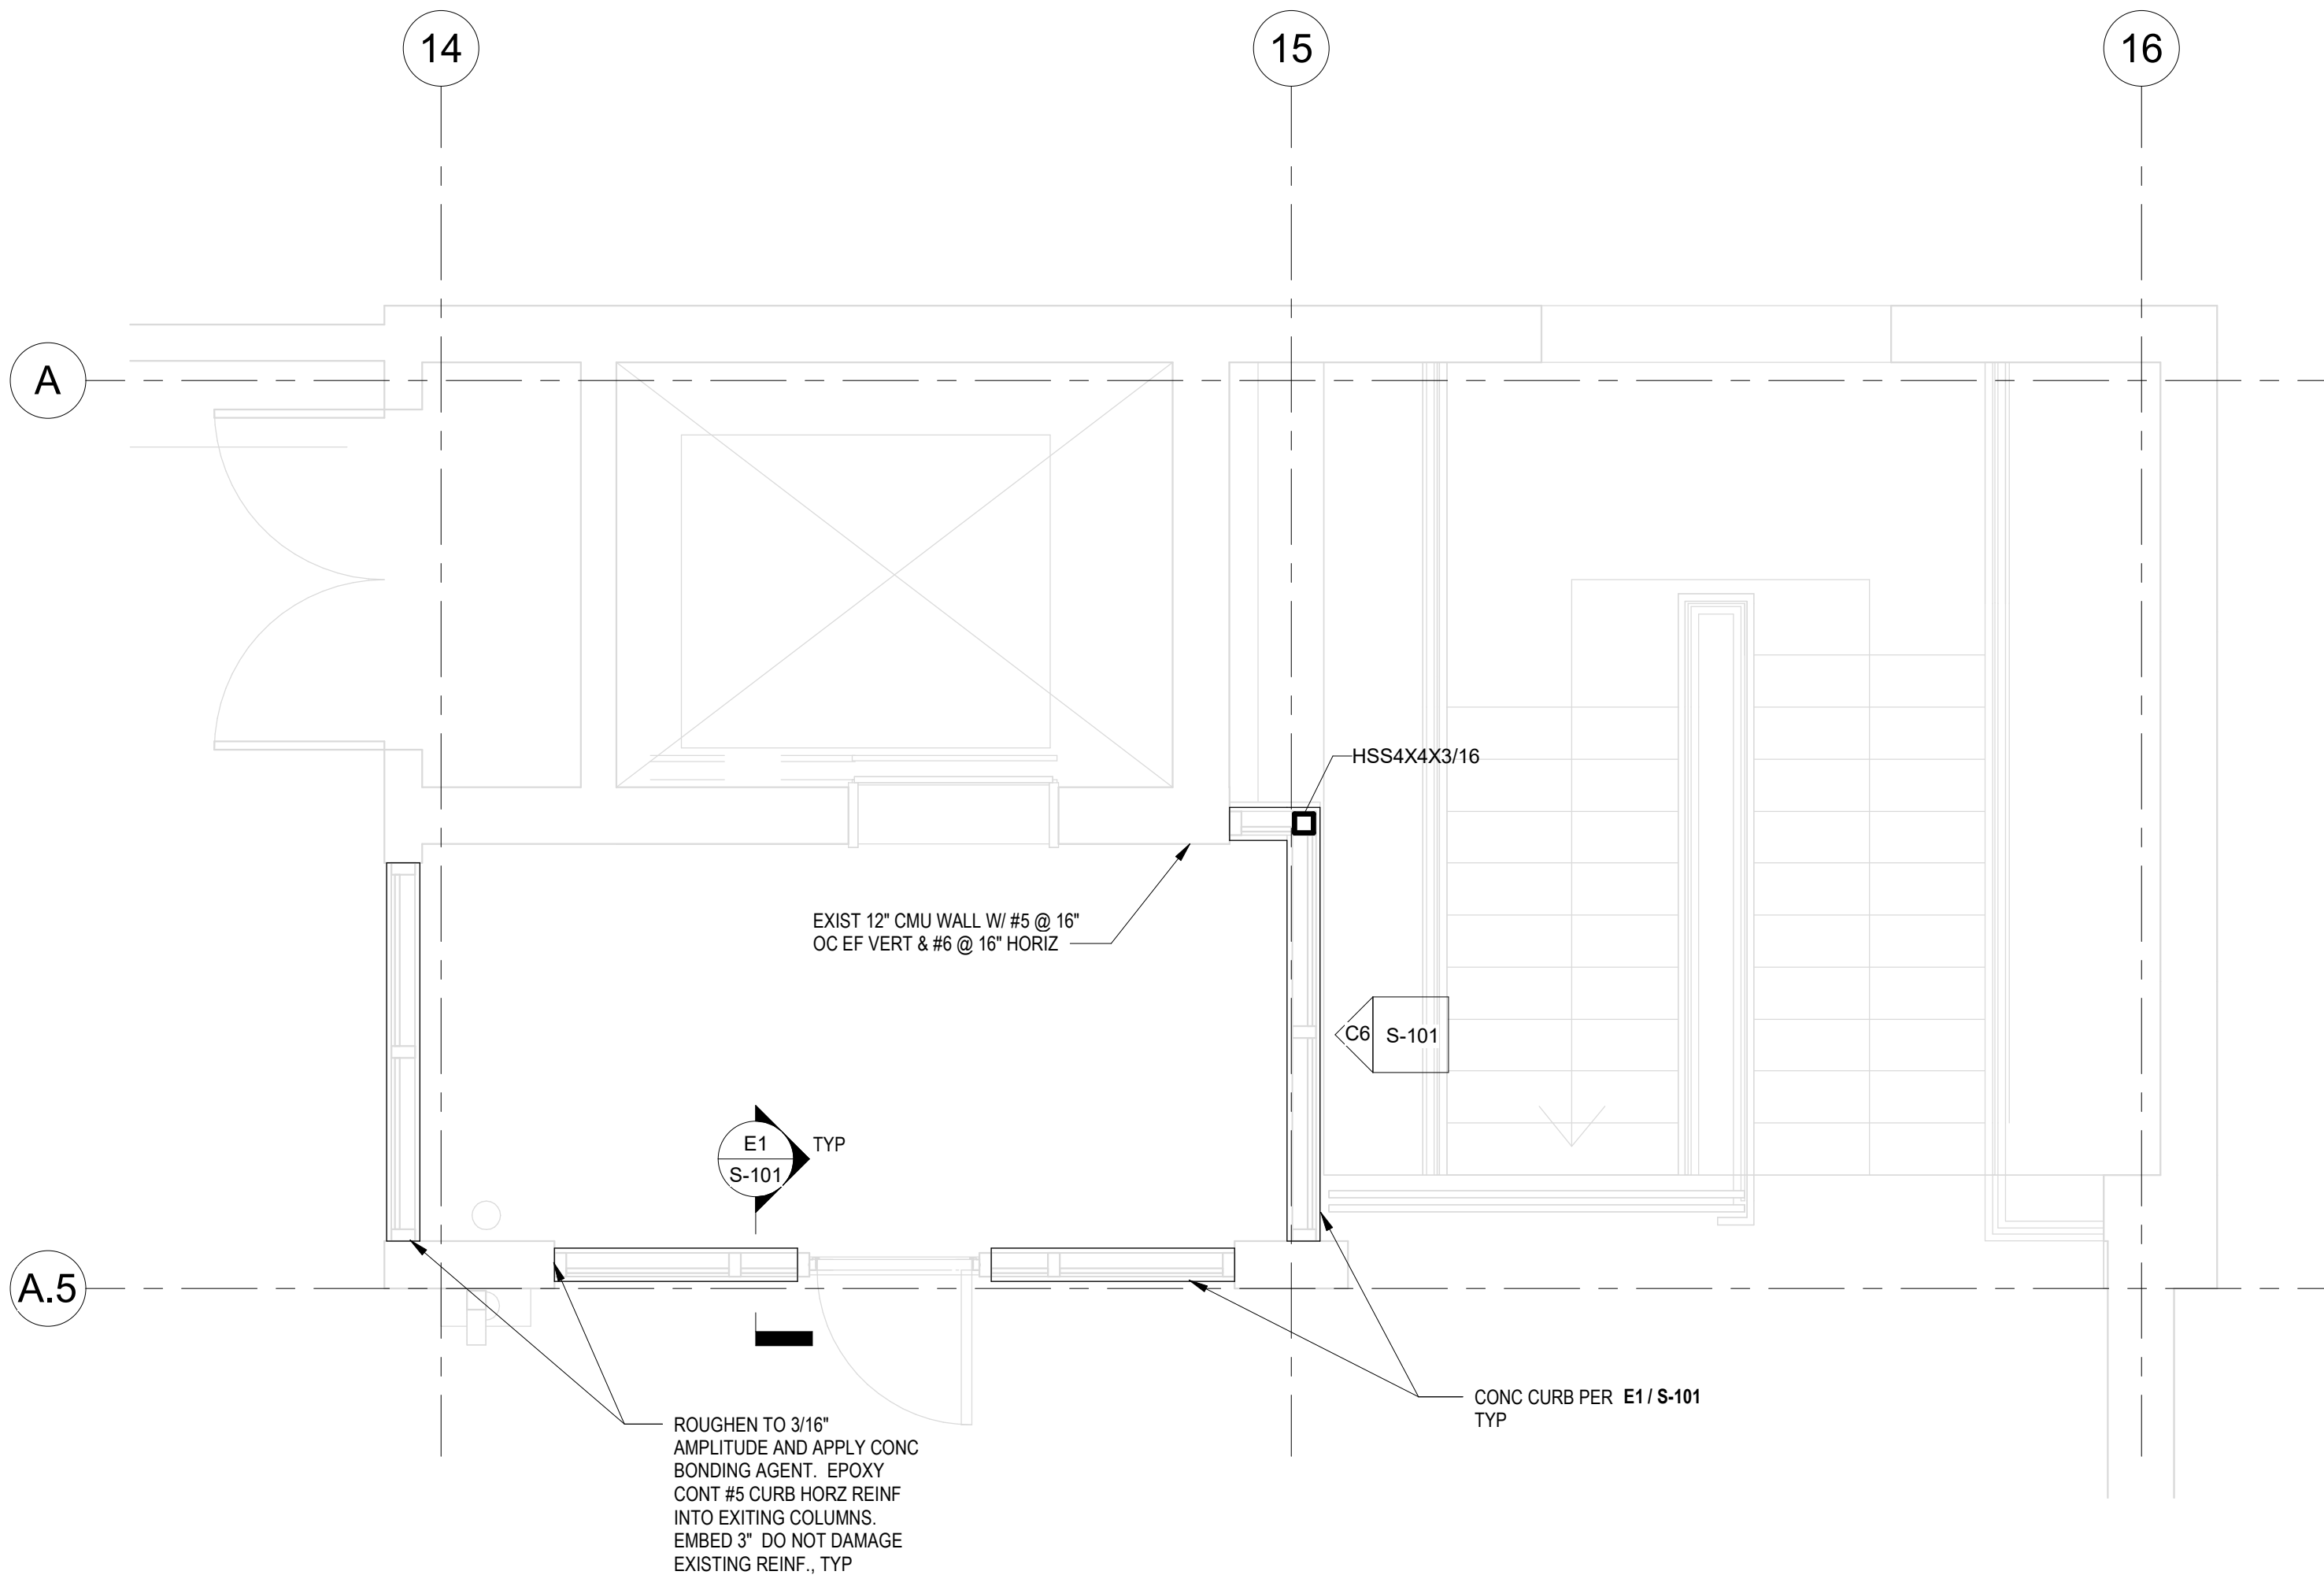


PLAN NOTES:

- REFER TO SHEETS S-001 AND S-002 FOR GENERAL NOTES. THESE NOTES & DETAILS ON THIS SHEET SHALL BE USED WHERE APPLICABLE, WHETHER SPECIFICALLY REFERENCED OR NOT.
- REFER TO ARCHITECTURAL AND MECHANICAL DRAWINGS FOR ANY DIMENSIONS, OPENINGS, AND ELEVATIONS NOT SHOWN.
- REFER TO ARCHITECTURAL AND MECHANICAL DRAWINGS FOR THE FOLLOWING:
A. DIMENSIONS NOT SHOWN.
B. OPENINGS NOT SHOWN.
C. FLOOR ELEVATIONS.
- FOR TYPICAL OPENINGS EXACT LOCATION AND SIZE. SEE ARCHITECTURAL AND MECHANICAL DRAWINGS.
- DIMENSIONS AND ELEVATIONS SHALL BE VERIFIED PRIOR TO STEEL FABRICATION AND ERECTION.

C1 LEVEL 4 - STRUCTURAL PLAN
3/8" = 1'-0"

C6 STRUCTURAL FRAME ELEVATION
3/8" = 1'-0"

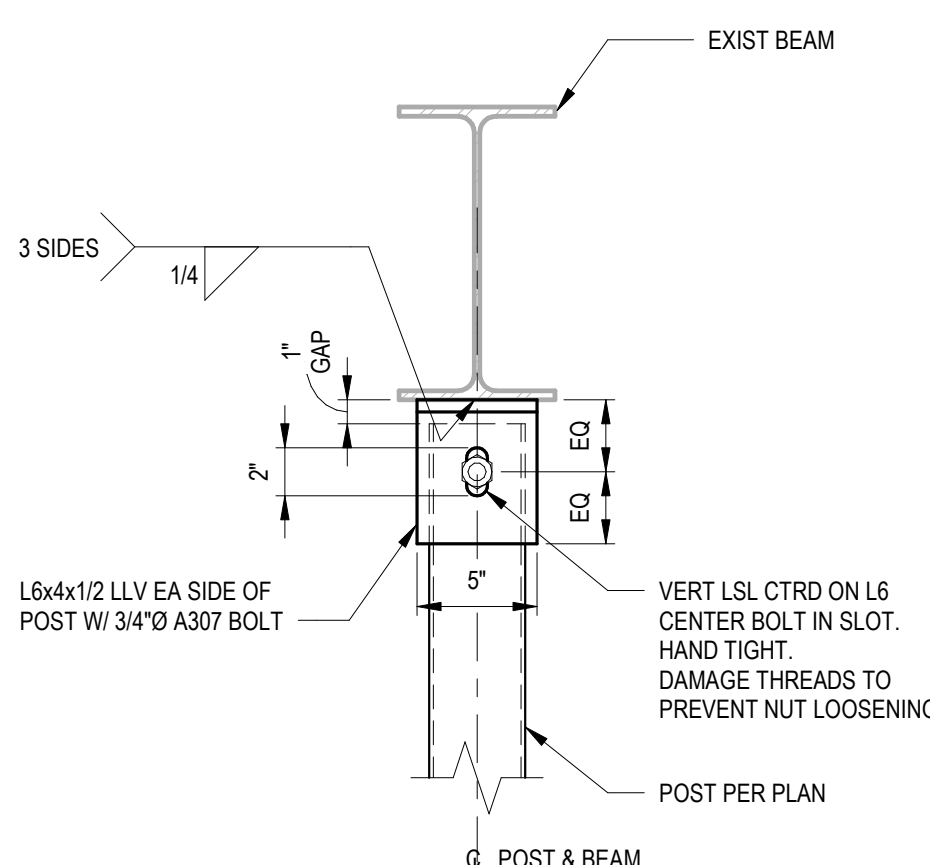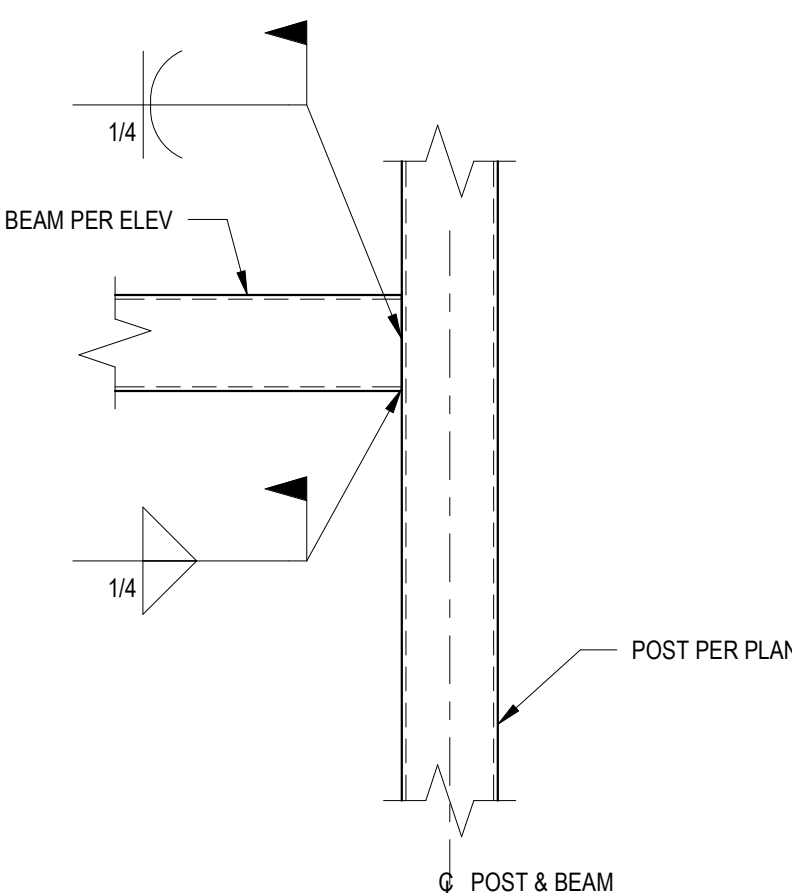
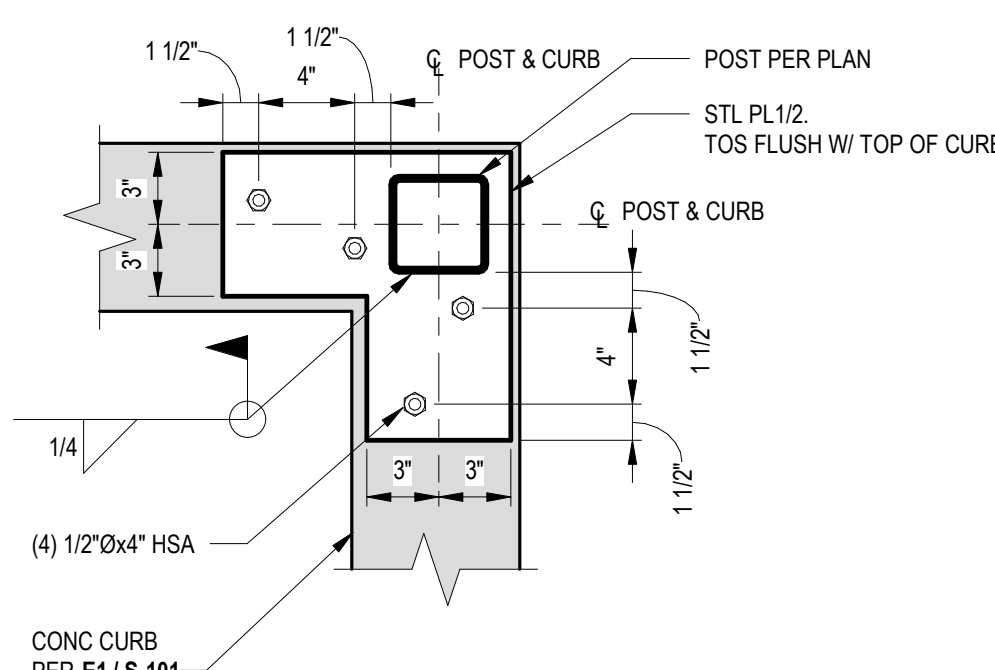
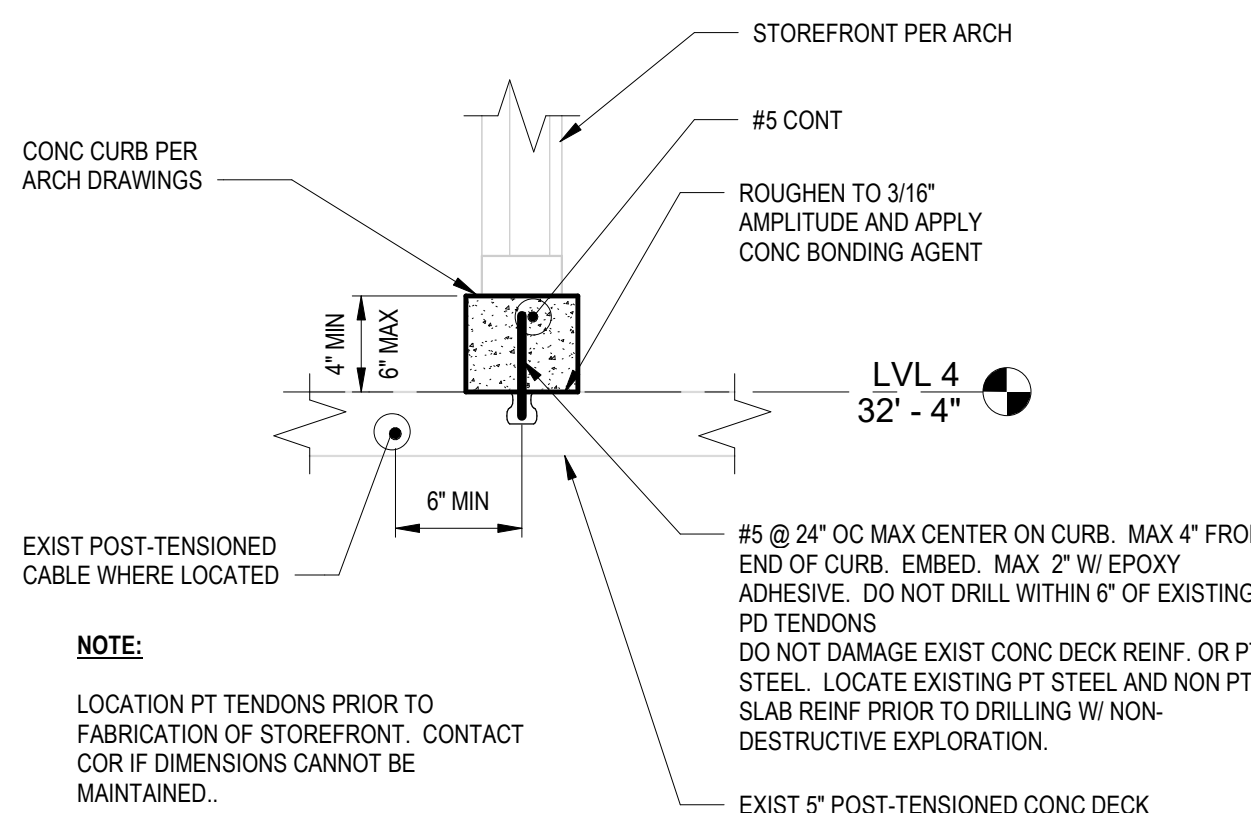


E1 CONC CURB DETAIL
1" = 1'-0"

E3 POST BASE
1 1/2" = 1'-0"

E5 TYP POST TO BEAM CONN
1 1/2" = 1'-0"

E7 POST TO EXIST CONN
1 1/2" = 1'-0"

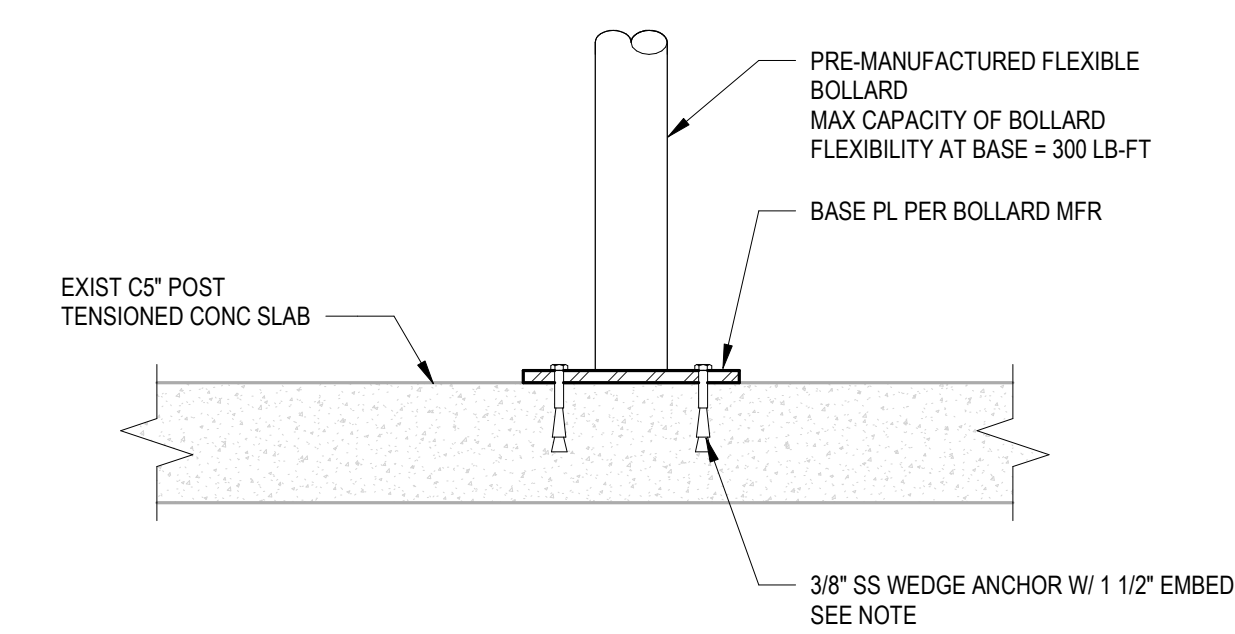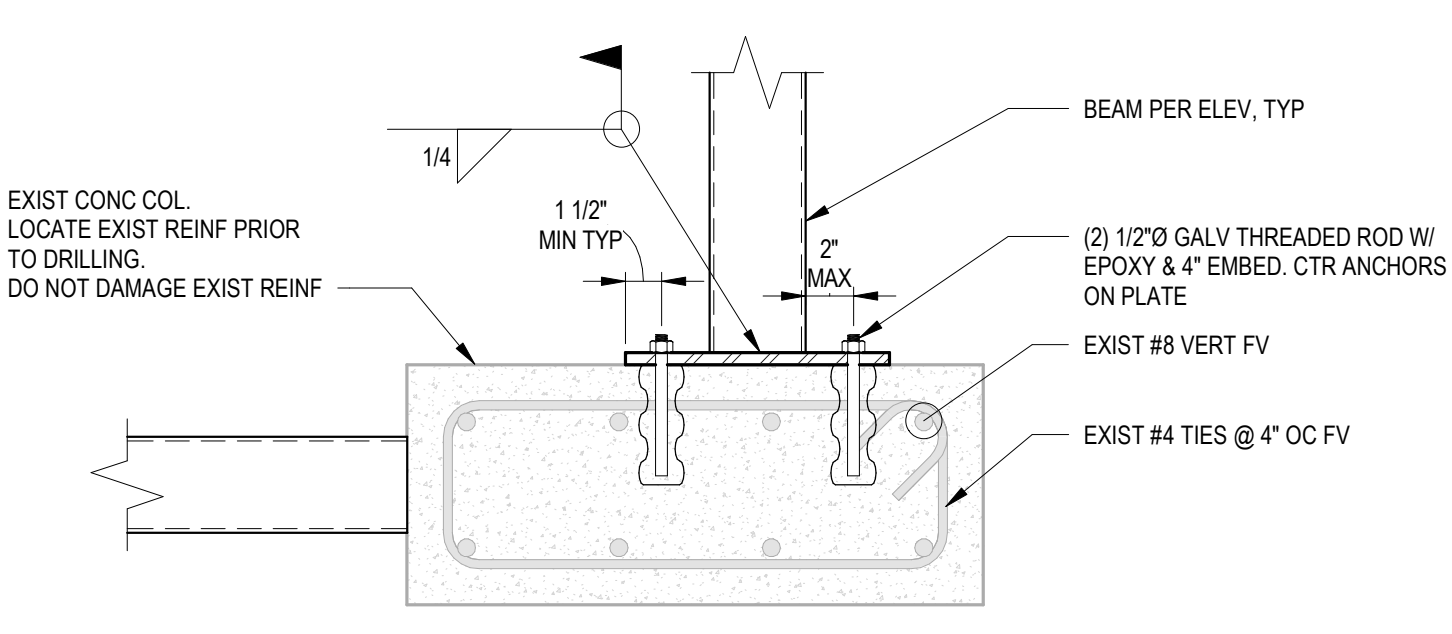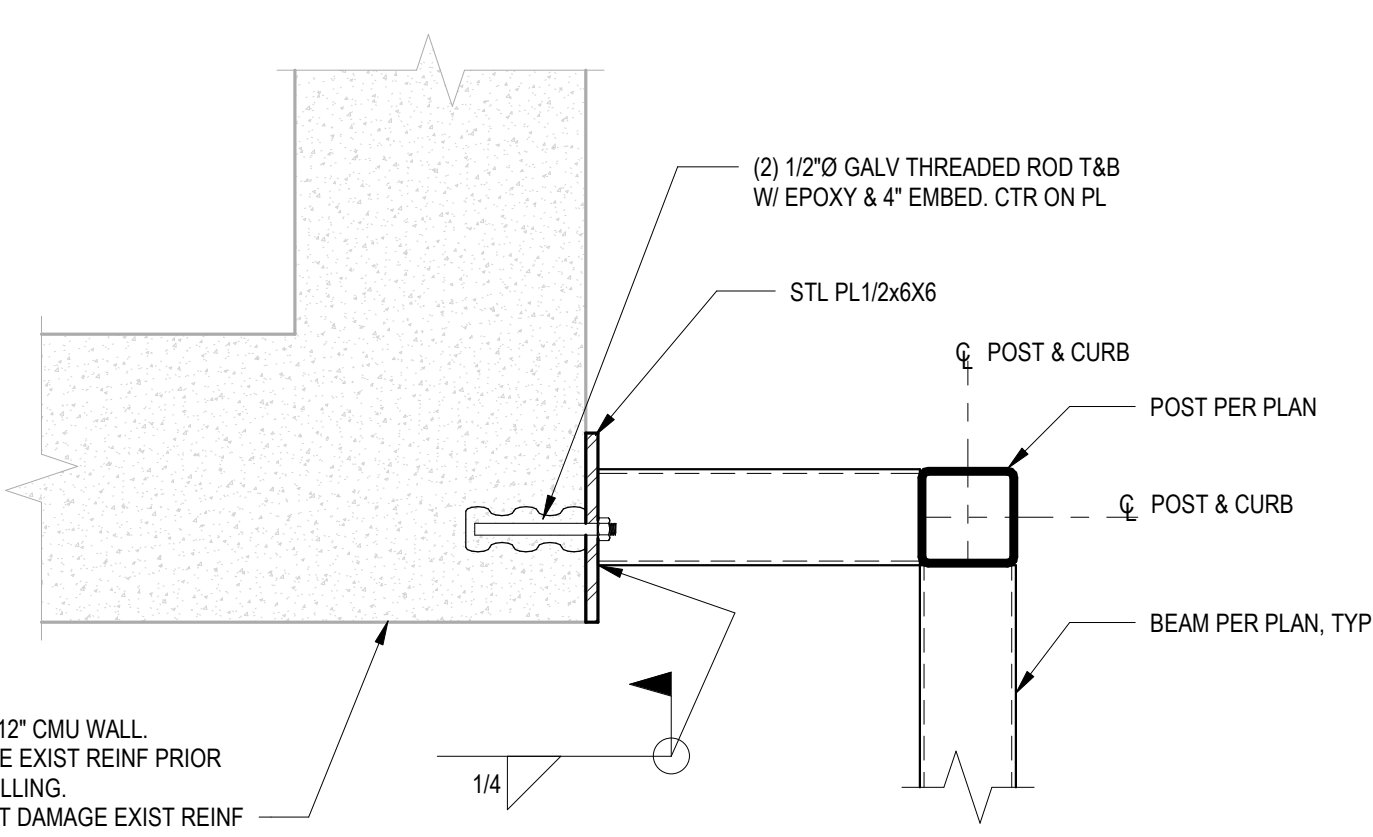

F3 BEAM TO EXIST WALL CONN
1 1/2" = 1'-0"


F5 BEAM TO EXIST CONC COL CONN
1 1/2" = 1'-0"

F7 BOLLARD TO EXIST SLAB CONN
1 1/2" = 1'-0"

KEY PLAN




AREA SHOWN

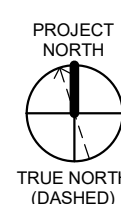

Revisions:	Date:

CONSULTANT
ENGINEERING DISCIPLINE:
wsp
WSP USA Inc.
1201 Pacific Ave
Suite 550
Tacoma, WA 98402
TEL: (206) 431-2300
FAX: (206) 431-2250

ARCHITECT/ENGINEER OF RECORD
A/E:
SPEEDS DESIGN BUILD
625 1ST AVE, STE 301
SEATTLE, WA 98104
(206) 590-2118
RAY SPEEDS

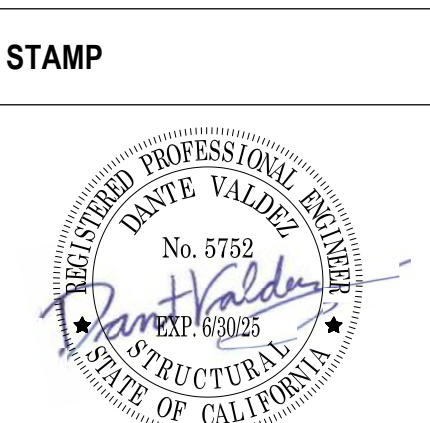

Office of
Capital Projects
VA U.S. Department
of Veterans Affairs

Drawing Title
LEVEL 4 - STRUCTURAL PLAN, DETAILS, AND ELEVATIONS
Approved:

Phase
100% CONSTRUCTION DOCUMENTS (CD)

Project Title
REPAIR AND WEATHERIZE PARKING STRUCTURE 211 ELEVATOR
Location
SAN FRANCISCO VA MEDICAL CENTER - SAN FRANCISCO, CA
Issue Date
11/17/2025
Checked
NRT
Drawn
JKM
Project Number
662-23-111
Building Number
211
Drawing Number
S-101

SD

STORM WATER

X

EXISTING PIPE TO BE REMOVED

DROP IN PIPE

WYE

DIRECTION OF PIPE PITCH (DOWN)

PIPE UP


PIPE DOWN

DETAIL NUMBER


DRAWING NUMBER WHERE DRAWN

POINT OF CONNECTION BETWEEN NEW AND EXISTING WORK


LIMIT OF DEMOLITION

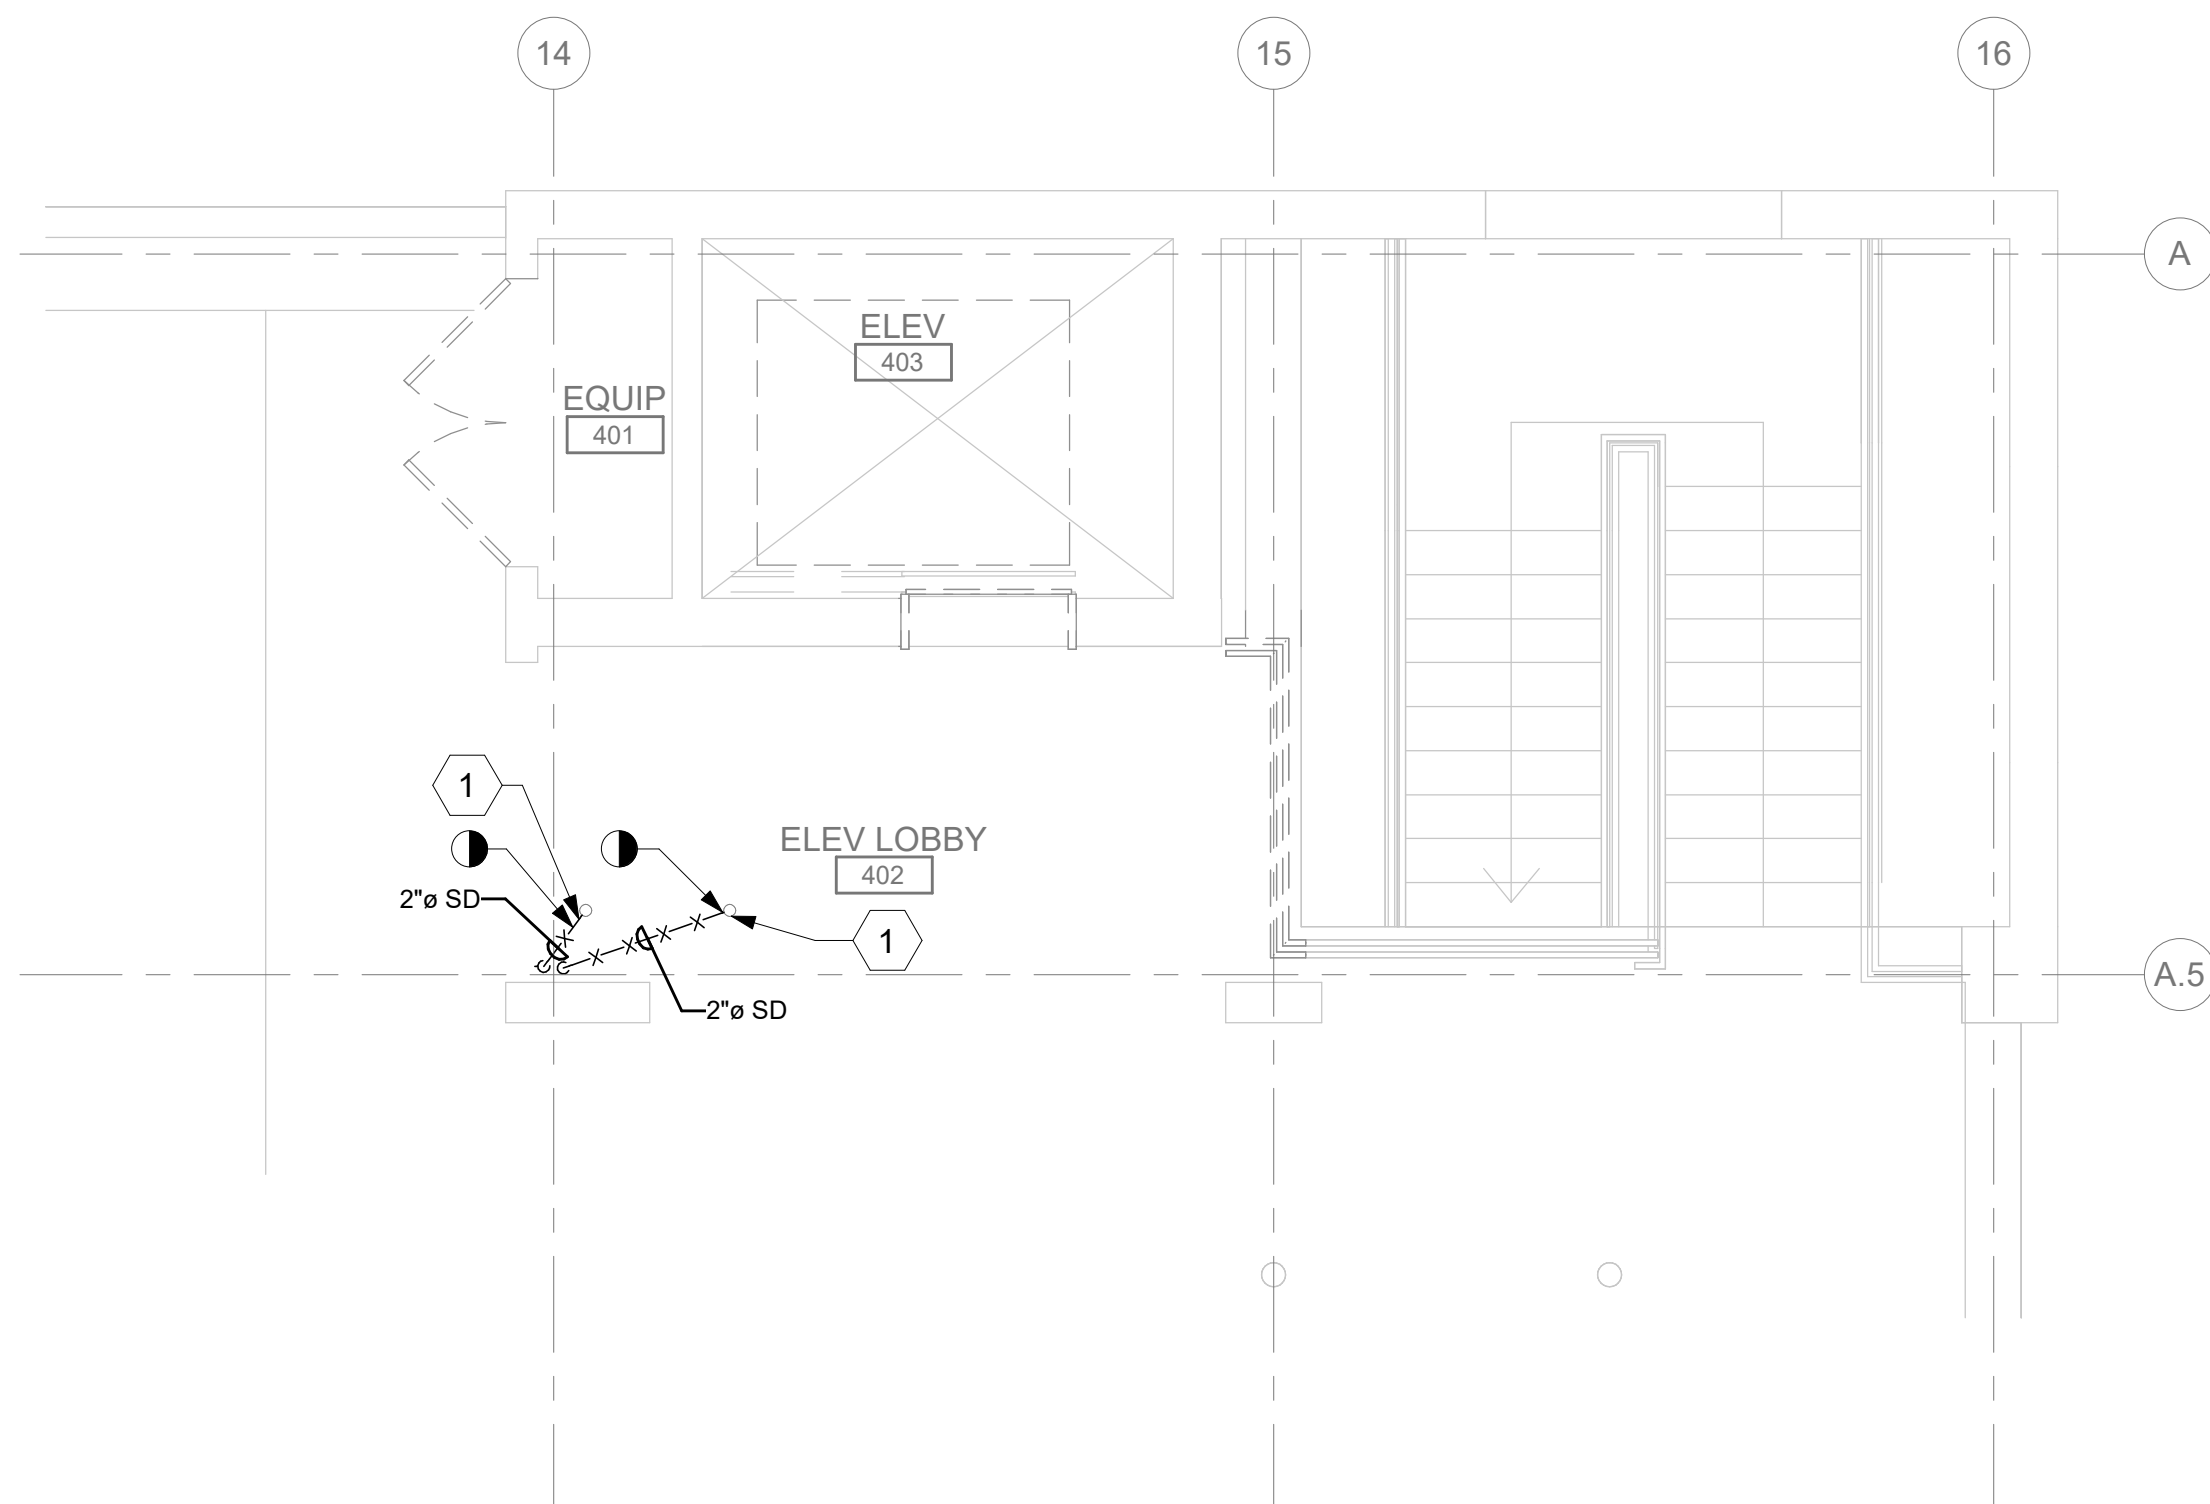

1 LEVEL 4 - PLUMBING DEMOLITION FLOOR PLAN
1/4" = 1'-0"

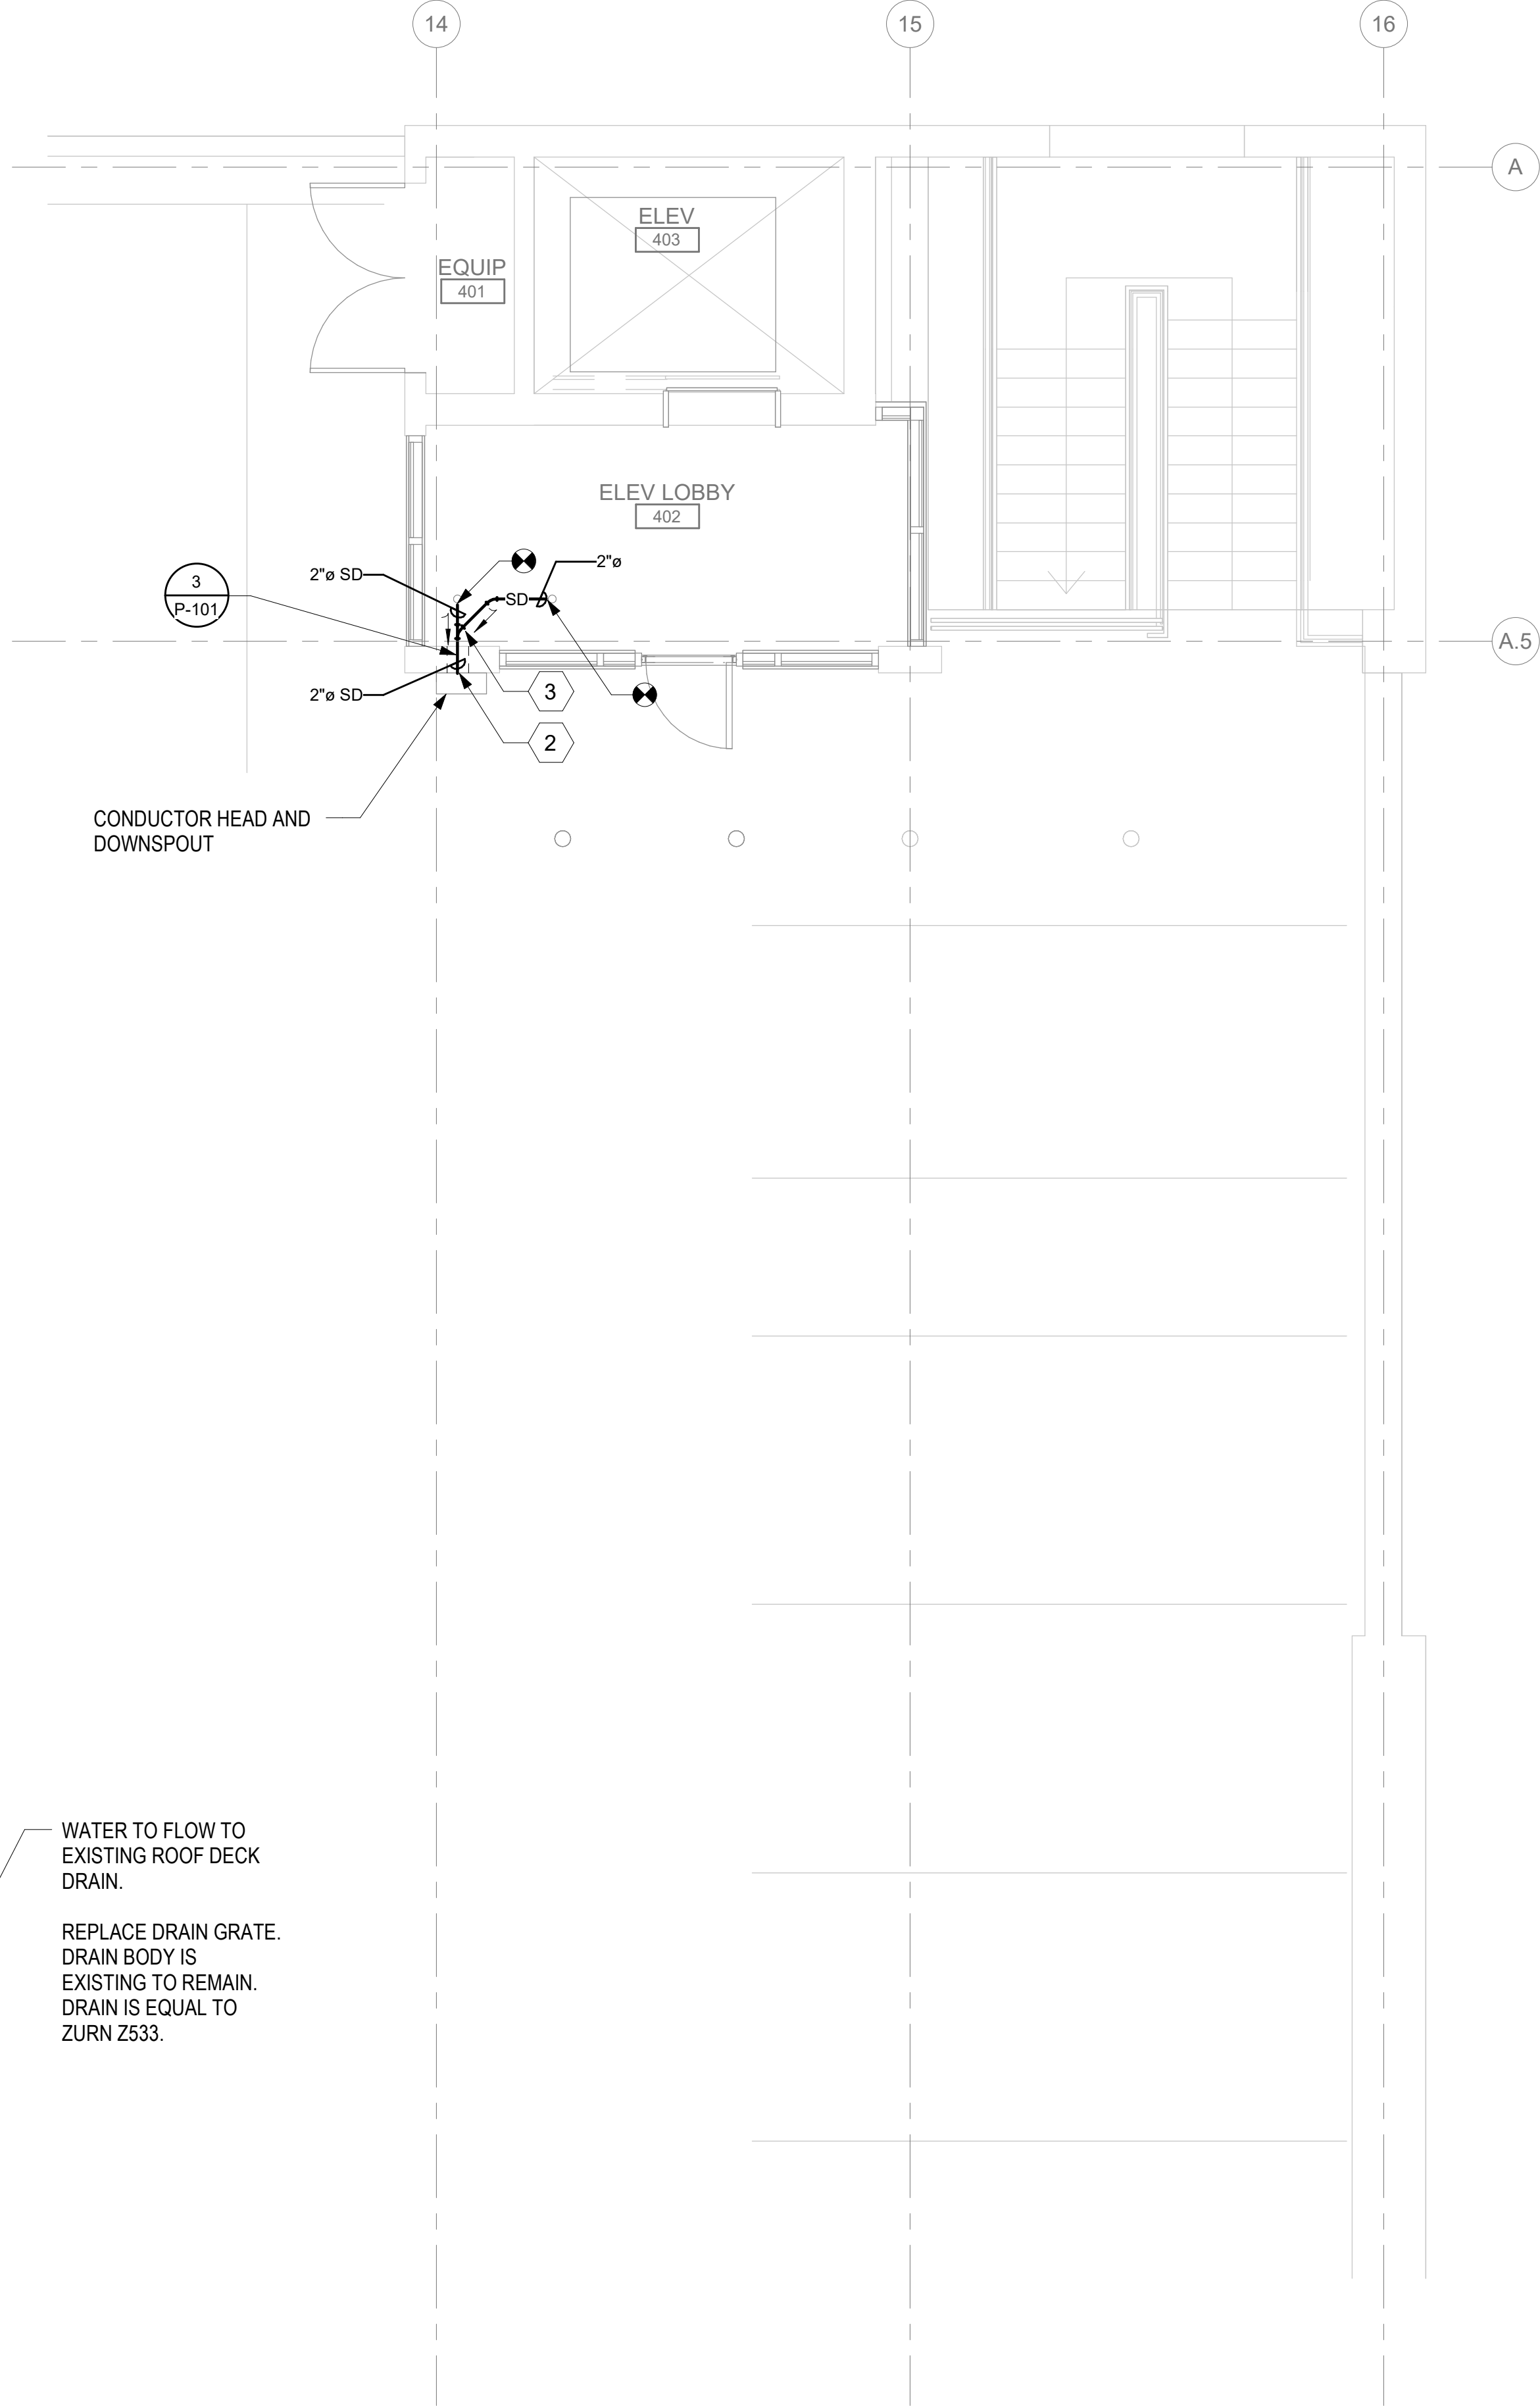

2 LEVEL 4 - PLUMBING FLOOR PLAN
1/4" = 1'-0"

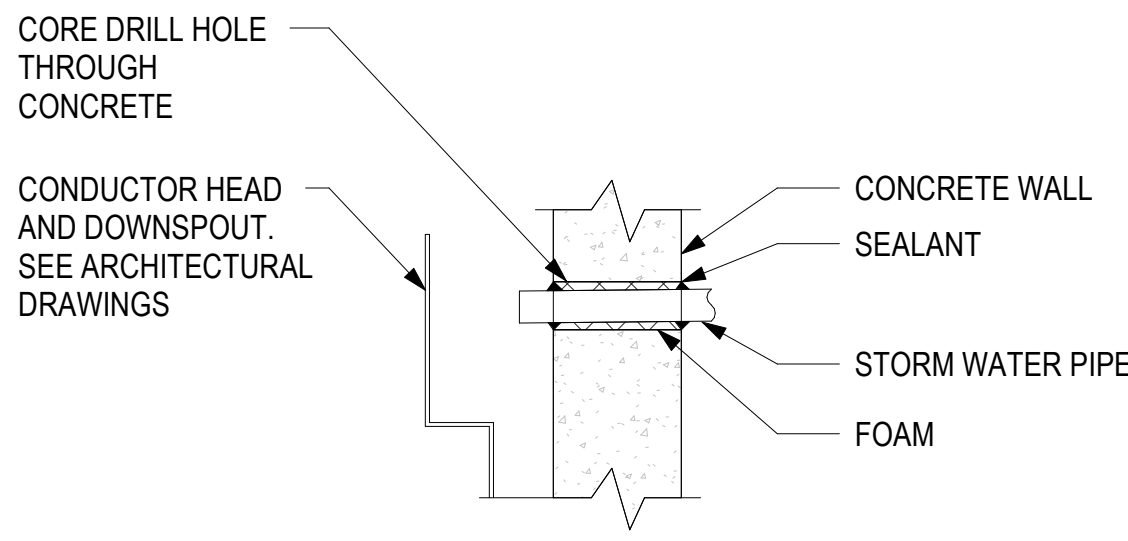

3 STORM WATER PIPE THROUGH CONCRETE WALL DETAIL
NTS

DEMOLITION GENERAL NOTES

1. REFER TO ALL DRAWINGS FOR COORDINATION BETWEEN DEMOLITION AND NEW WORK. COORDINATE DEMOLITION WORK WITH THAT OF OTHER TRADES.

2. CONTRACTOR SHALL BE RESPONSIBLE FOR THE FOLLOWING:

A. PROTECTING, COVERING, AND SEALING EXISTING EQUIPMENT AND SURROUNDINGS DURING DEMOLITION FROM DIRT, DUST, AND DEBRIS.

B. ENSURING THE SAFE PASSAGE OF PERSONS IN AND AROUND THE BUILDING DURING DEMOLITION.

C. PREVENTING INJURY TO PERSONS AND DAMAGE TO PROPERTY. PROVIDING ADEQUATE SHORING AND BRACING TO PREVENT COLLAPSE.

D. REPAIRING DAMAGED PROPERTY TO ITS ORIGINAL CONDITION IMMEDIATELY AFTER THE DAMAGE OCCURS.

E. TAKING EFFECTIVE MEASURES TO PREVENT DUST MIGRATION.

3. MAINTAIN ALL UTILITIES EXCEPT THOSE REQUIRING REMOVAL OR RELOCATION. KEEP UTILITIES IN SERVICE AND PROTECT FROM DAMAGE. DO NOT INTERRUPT UTILITIES SERVING AREAS OUTSIDE OF PRESENT SCOPE WITHOUT FIRST OBTAINING PERMISSION FROM OWNER. PROVIDE TEMPORARY SERVICES AS REQUIRED.

GENERAL NOTES

1. CONTRACTOR MUST VERIFY ALL DIMENSIONS BY FIELD MEASUREMENT BEFORE BEGINNING ANY FABRICATION OR CONSTRUCTION.

2. ALL WORK SHALL BE IN ACCORDANCE WITH APPLICABLE CODES, VA STANDARDS, AND SPECIFICATIONS.

3. CONTRACTOR SHALL INSTALL ALL EQUIPMENT IN STRICT ACCORDANCE WITH MANUFACTURER'S RECOMMENDATIONS. IN CASES OF CONFLICT BETWEEN MANUFACTURER REQUIREMENTS, DRAWINGS, OR SPECIFICATIONS, THE MORE STRINGENT REQUIREMENT SHALL GOVERN.

4. COORDINATE INSTALLATION OF EQUIPMENT AND MATERIALS WITH OTHER TRADES.

5. DO NOT ROUTE PIPING OVER ELECTRICAL PANELS OR ELECTRONIC EQUIPMENT.

6. CONTRACTOR SHALL COORDINATE WITH GENERAL CONTRACTOR AND VA COR PRIOR TO ANY CUTTING OF WALLS AND ROOF.

7. INSTALL ALL STORM WATER PIPING WITH A MINIMUM OF 1/4" PER LINEAR FOOT (2%) SLOPE.

KEYNOTES

1. DEMO EXISTING ROOF STORM WATER AND OVERFLOW PIPING UP TO ROOF DRAIN RISER CONNECTION.

2. CORE DRILL THROUGH EXISTING WALL. ROUTE STORM WATER PIPING TO DRAIN INTO CONDUCTOR HEAD AND ASSOCIATED GUTTER. SEE ARCHITECTURAL PLANS FOR FURTHER INFORMATION.

3. INSULATE STORM WATER PIPING IN ACCORDANCE WITH SPECIFICATION SECTION 22 07 11.

KEY PLAN

AREA OF WORK

AREA SHOWN

		CONSULTANT/ DISCIPLINE	ARCHITECT/ ENGINEER OF RECORD	STAMP	Office of Capital Projects	Drawing Title PLUMBING FLOOR PLANS	Phase 100% CONSTRUCTION DOCUMENTS	Project Title REPAIR AND WEATHERIZE PARKING STRUCTURE 211 ELEVATOR	Project Number 662-23-111
		DISCIPLINE:	A/E: SPEES DESIGN BUILD 23830 PACIFIC HIGHWAY S. SUITE 300 KENT, WA 98032			Approved:		Location VA MEDICAL CENTER - SAN FRANCISCO, CA	Building Number 211
Revisions:		Date:			U.S. Department of Veterans Affairs			Issue Date 11/17/2025	Drawing Number P-101
								Checked MGH/JW	
								Drawn TGJM/CY	

VA FORM 08 - 6231 1 11/10/2025 1:50:33 PM 2
Autodesk Docs://SDB VA CA SF
6221 Elevator
662-23-111/VASF_B221
Elevator_ME_SDB.rvt


1	2	3	4	5	6	7	8	9	10
ABBREVIATIONS				GENERAL NOTES				SHEET INDEX	
A B C D E F 1PH 1P 2/C 3/C 3PH 4/C 4W A/C A/E AAP AC ACC ADDL ADJ AF AFC 5 6 

[illegible]

7	8	9	10		
GENERAL SYMBOL					
SCALE SECTION LETTER SECTION SHEET WHERE SECTION IS TAKEN FROM SECTION LETTER SHEET WHERE SECTION IS TAKEN FROM DETAIL NUMBER SHEET ON WHICH DETAIL APPEARS DETAIL AREA IF PHOTO, ARROW DENOTES DIRECTION TAKEN FIGURE OR PHOTO DETAIL NUMBER SHEET WHERE DETAIL IS TAKEN FROM DETAIL/PLAN NUMBER 1 XXX A XXX 1 XXX 2 XXX 1 - DETAIL/PLAN		XXX CONDUIT & WIRE TAG (REFER TO CONDUIT AND WIRE SCHEDULE) XX FAULT CURRENT TAG (3 PH, SYM AMPS) 1 KEY NOTE 01 METERING NOTE ////// CONDUIT OR EQUIPMENT TO BE REMOVED ----- CONDUIT CONCEALED IN WALL, CEILING, UNDER FLOOR, IN FLOOR SLAB, OR ROUTED UNDERGROUND ----- CONDUIT CONCEALED WHERE POSSIBLE, OTHERWISE EXPOSED ~~~~~ EXTRA-HARD USAGE FLEXIBLE CORD ~~~~~ FLEXIBLE CONDUIT ○ CONDUIT TURNED UP OR TOWARD ○ CONDUIT TURNED DOWN OR AWAY ┐ CONDUIT CAPPED			
CIRCUITING DESIGNATIONS					
WHERE A PANEL NAME OR TICK MARKS LEADING TO PANEL BOARD AND CORRESPONDING CIRCUIT ARE CALLED OUT ADJACENT TO A RECEPTACLE, LUMINAIRE, OR MISC LOAD, THAT LOAD SHALL BE CIRCUITED TO THE CORRESPONDING PANELBOARD CIRCUIT BREAKER. CONDUIT AND WIRE FOR CIRCUIT SHALL BE 3/4" CONDUIT WITH (2) 12 AWG AND (1) 12 AWG GND, UNLESS OTHERWISE NOTED; IF FURTHER THAN 70', PHASE AND GROUND WIRE SHALL BE UPSIZED TO 10 AWG TO ACCOUNT FOR VOLTAGE DROP. SEE EXAMPLES BELOW:					
RECEPTACLE: PANELBOARD OR POWER SOURCE NAME = "P1" CIRCUIT NUMBER OF POWER SOURCE = "2"					
LUMINAIRE: PANELBOARD OR POWER SOURCE NAME = "PP3" CIRCUIT NUMBER OF POWER SOURCE = "4" TYP LUMINAIRE TAG NAME, REFERENCE LUMINAIRE SCHEDULE = "L1" LIGHTING CONTROL SWITCH LEG = "a" ALL LUMINAIRES IN SAME ROOM ARE CIRCUITED TO SAME CIRCUIT = PP3-4					
MISC LOAD: PANELBOARD OR POWER SOURCE NAME = "PP" CIRCUIT NUMBER OF POWER SOURCE = "7"					
CONDUIT 3/4"C, 3#12 PHASE, 1#12 N, & 1#12 GND UNLESS SHOWN OTHERWISE, (EXAMPLE SHOWN: TO PANEL P1, CIRCUIT 1.3.5). LONG TICK FOR NEUTRAL WIRE; ONE SHORT TICK FOR EACH PHASE WIRE; GROUND SIZED PER NEC. NOTE THAT A SECOND SHORT TICK FOR LUMINAIRES IS FOR A TRAVELER WIRE. CONDUIT HOME RUN - SEE CONDUIT AND WIRE SCHEDULE					

 | | || THESE ARE GENERAL LEGENDS. NOT ALL SYMBOLS MAY BE SHOWN. REFERENCE PLANS FOR ALL UTILIZED SYSYMBOLS. | | | |

1	2	3	4	5	6	7	8	9	10
---	---	---	---	---	---	---	---	---	----

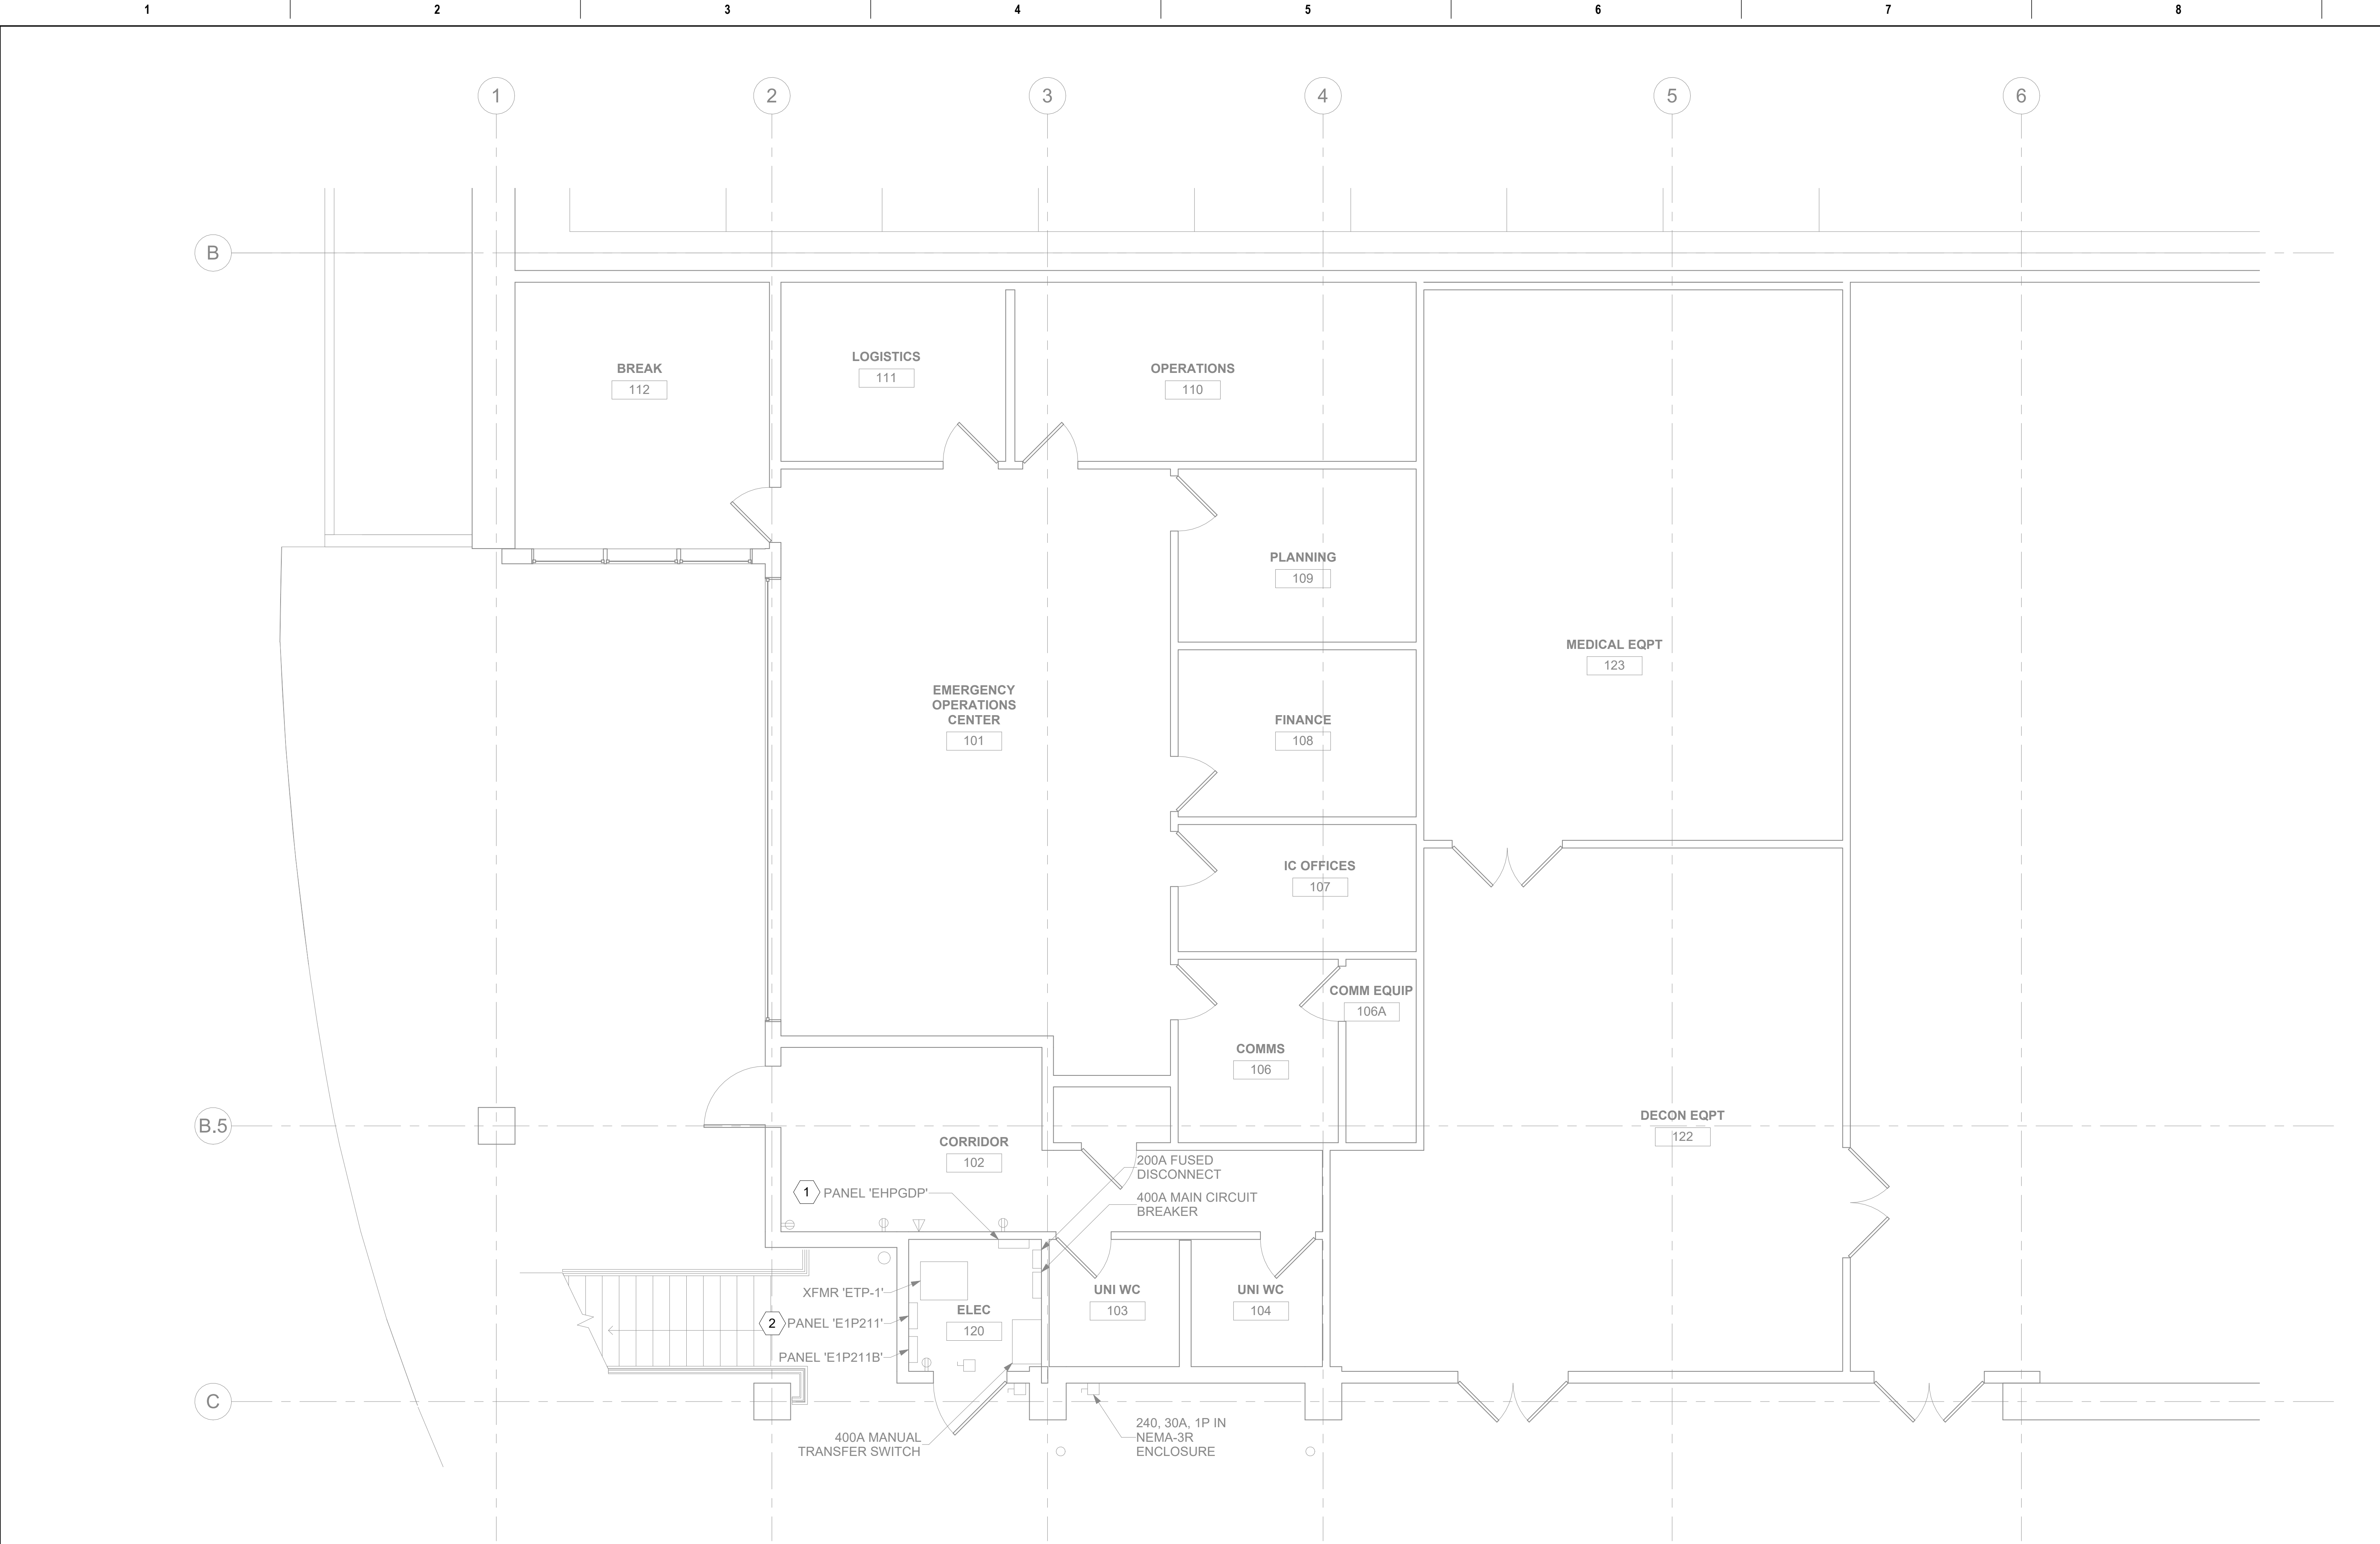

- GENERAL NOTES
1.

ALL EXISTING EQUIPMENT MAY NOT BE SHOWN FOR CLARITY. CONTRACTOR SHALL FIELD VERIFY ALL POWER, LIGHTING AND ASSOCIATED CIRCUITRY AS REQUIRED. ALL RACEWAYS AND CONDUCTORS ASSOCIATED WITH EQUIPMENT TO BE DEMOLISHED SHALL BE DEMOLISHED BACK TO THEIR SOURCE, UNLESS OTHERWISE NOTED.
2.

SEAL ALL INTERIOR WALL AND CEILING PENETRATIONS TO MATCH EXISTING FIRE RATING OR NEW FIRE RATING, IF REQUIRED. COORDINATE WITH ARCHITECTURAL DRAWINGS AS REQUIRED.
3.


CONTRACTOR SHALL PROVIDE UPDATED CIRCUIT PANEL DIRECTORIES FOR ALL PANELS THAT CONTAIN CIRCUITS IMPACTED BY THIS PROJECT.
4.

CONTRACTOR SHALL PROVIDE PULL BOXES FOR ALL FEEDERS WHERE FEEDER RUNS EXCEED 250FT OR HAVE MORE THAN 270 DEGREES OF TOTAL BEND. PULLBOX PLACEMENT AND SIZING BY CONTRACTOR. COORDINATE PULLBOX LOCATIONS WITH ALL OBSTRUCTIONS, TRADES, AND VA AS REQUIRED.

- KEY NOTES
- 1

PANELBOARD CONTAINING LIGHTING CIRCUIT TO BE MODIFIED. REFERENCE SHEET E-104 FOR ADDITIONAL INFORMATION.
- 2

PANELBOARD CONTAINING RECEPTACLE CIRCUIT TO BE MODIFIED. REFERENCE SHEET E-104 FOR ADDITIONAL INFORMATION.

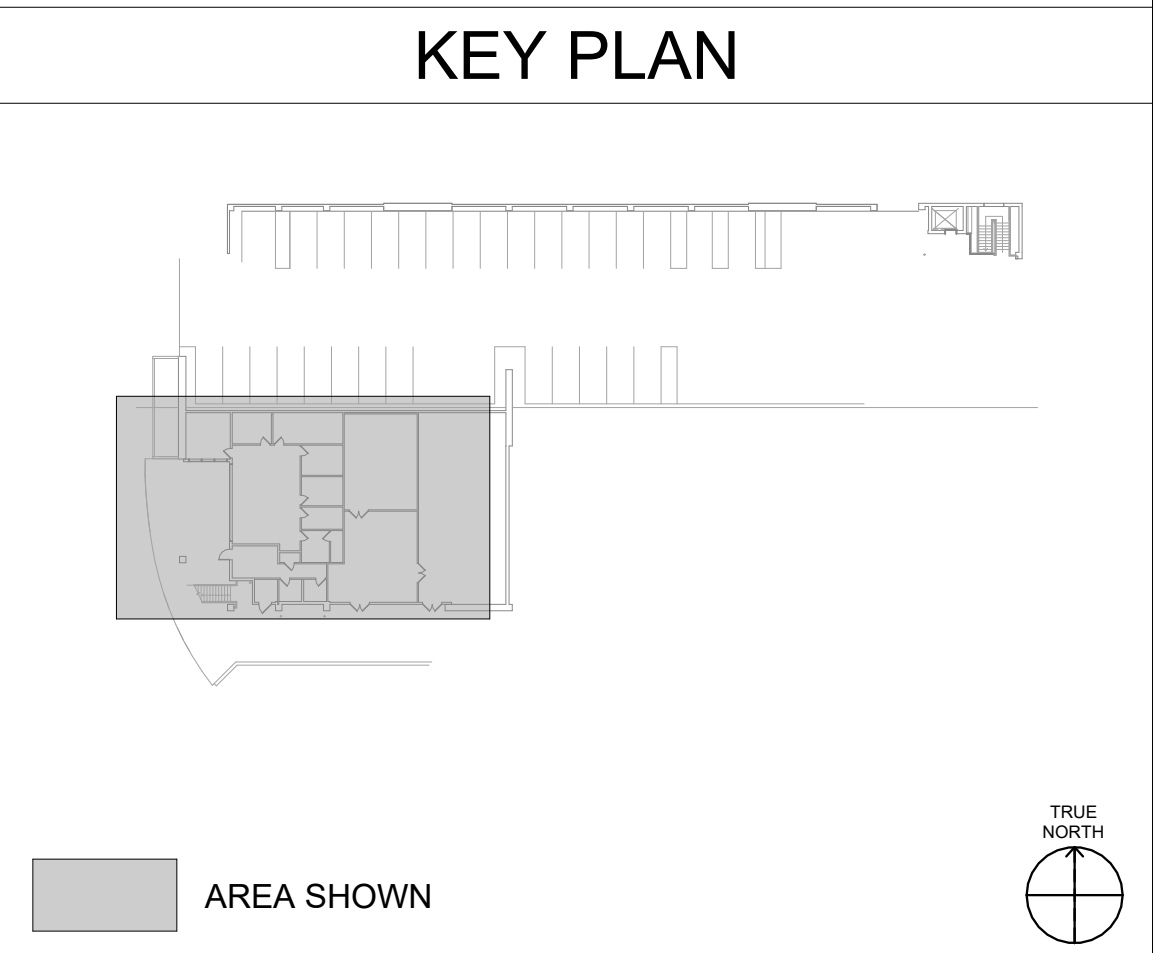

1

ELECTRICAL FLOOR PLAN - LEVEL 1

1/4" = 1'-0"



		CONSULTANT/ DISCIPLINE	ARCHITECT/ ENGINEER OF RECORD	STAMP	Office of Construction and Facilities Management	Drawing Title	Phase	Project Title	Project Number
		DISCIPLINE:	A/E: SPEES DESIGN BUILD 23830 PACIFIC HIGHWAY S. SUITE 300 KENT, WA 98032			ELECTRICAL FLOOR PLAN - LEVEL 1	100% CONSTRUCTION DOCUMENTS	REPAIR AND WEATHERIZE PARKING STRUCTURE 211 ELEVATOR	662-23-111
					VA U.S. Department of Veterans Affairs	Approved:	FULLY SPRINKLERED	Location SAN FRANCISCO VA MEDICAL CENTER - SAN FRANCISCO, CA	Building Number 211
									Issue Date 11/17/2025
Revisions:		Date:						Checked DCW	Drawn JFO/ONI


GENERAL NOTES

- ALL EXISTING EQUIPMENT MAY NOT BE SHOWN FOR CLARITY. CONTRACTOR SHALL FIELD VERIFY ALL POWER, LIGHTING AND ASSOCIATED CIRCUITRY AS REQUIRED. ALL RACEWAYS AND CONDUCTORS ASSOCIATED WITH EQUIPMENT TO BE DEMOLISHED SHALL BE DEMOLISHED BACK TO THEIR SOURCE, UNLESS OTHERWISE NOTED.
- SEAL ALL INTERIOR WALL AND CEILING PENETRATIONS TO MATCH EXISTING FIRE RATING OR NEW FIRE RATING, IF REQUIRED. COORDINATE WITH ARCHITECTURAL DRAWINGS AS REQUIRED.
- CONTRACTOR SHALL PROVIDE UPDATED CIRCUIT PANEL DIRECTORIES FOR ALL PANELS THAT CONTAIN CIRCUITS IMPACTED BY THIS PROJECT.
- CONTRACTOR SHALL PROVIDE PULL BOXES FOR ALL FEEDERS WHERE FEEDER RUNS EXCEED 250FT OR HAVE MORE THAN 270 DEGREES OF TOTAL BEND. PULLBOX PLACEMENT AND SIZING BY CONTRACTOR. COORDINATE PULLBOX LOCATIONS WITH ALL OBSTRUCTIONS, TRADES, AND VA AS REQUIRED.

KEY NOTES

- EXISTING LIGHT FIXTURE TO BE DEMOLISHED AND REPLACED. CONTRACTOR SHALL PERFORM CIRCUIT TRACING TO IDENTIFY EXACT CIRCUIT CONTAINING REPLACEMENT LIGHT FIXTURE. CONTRACTOR SHALL UPDATE CIRCUIT DIRECTORY AS APPLICABLE. CIRCUIT DIRECTORY SHALL BE PRINTED AND NOT HANDWRITTEN.
- EXISTING RECEPTACLE TO BE DEMOLISHED AND REPLACED. CONTRACTOR SHALL PERFORM CIRCUIT TRACING TO IDENTIFY EXACT CIRCUIT CONTAINING REPLACEMENT GROUND FAULT CIRCUIT INTERRUPTER RECEPTACLE. CONTRACTOR SHALL UPDATE CIRCUIT DIRECTORY AS APPLICABLE. CIRCUIT DIRECTORY SHALL BE PRINTED AND NOT HANDWRITTEN.
- EXTEND EXISTING CONDUIT AND WIRE FOR LIGHTING CIRCUIT TO PROVIDED FIXTURES AS SHOWN. CONTRACTOR SHALL PERFORM CIRCUIT TRACING TO IDENTIFY EXACT CIRCUIT TO BE MODIFIED. CONTRACTOR SHALL UPDATE CIRCUIT DIRECTORY AS APPLICABLE. CIRCUIT DIRECTORY SHALL BE PRINTED AND NOT HANDWRITTEN.

KEY PLAN

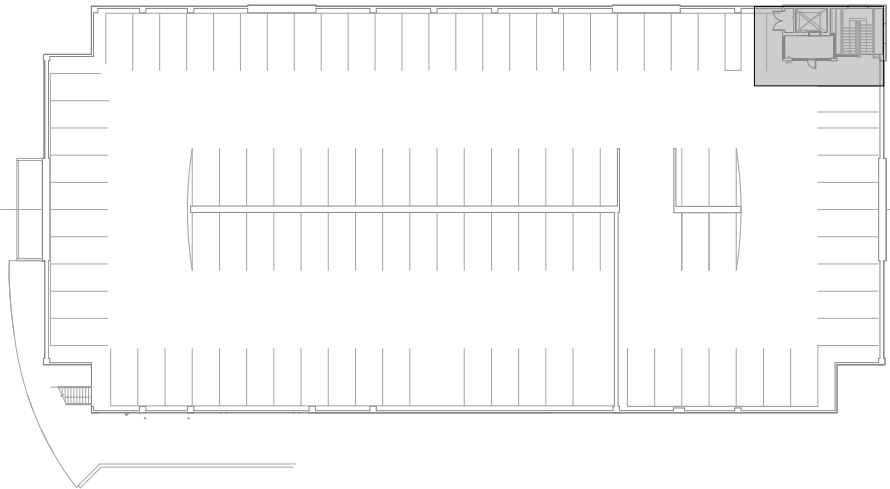

AREA SHOWN




1 ELECTRICAL FLOOR PLAN - LEVEL 4
1/2" = 1'-0"



		CONSULTANT/ DISCIPLINE		ARCHITECT/ ENGINEER OF RECORD		STAMP		Office of Construction and Facilities Management		Drawing Title		Phase		Project Title		Project Number	
		DISCIPLINE:		A/E: SPEES DESIGN BUILD 23830 PACIFIC HIGHWAY S. SUITE 300 KENT, WA 98032						ELECTRICAL FLOOR PLAN - LEVEL 4		100% CONSTRUCTION DOCUMENTS		REPAIR AND WEATHERIZE PARKING STRUCTURE 211 ELEVATOR		662-23-111	
				Approved:						FULLY SPRINKLERED		Location SAN FRANCISCO VA MEDICAL CENTER - SAN FRANCISCO, CA		Building Number 211			
												Issue Date 11/17/2025		Drawing Number E-104			
												Checked DCW					
												Drawn JFO/ONI					
Revisions:		Date:															

1. MODIFY CHAIN LENGTH TO PROVIDE MOUNTING HEIGHT AS REQUIRED ON DRAWINGS. (9'-6" A.F.F. TO BOTTOM OF LUMINAIRE UNLESS OTHERWISE NOTED OR REQUIRED).
2. PROVIDE TWO CHAIN HANGERS FOR EACH LUMINAIRE, ADJUST TO HANG LUMINAIRE LEVEL.

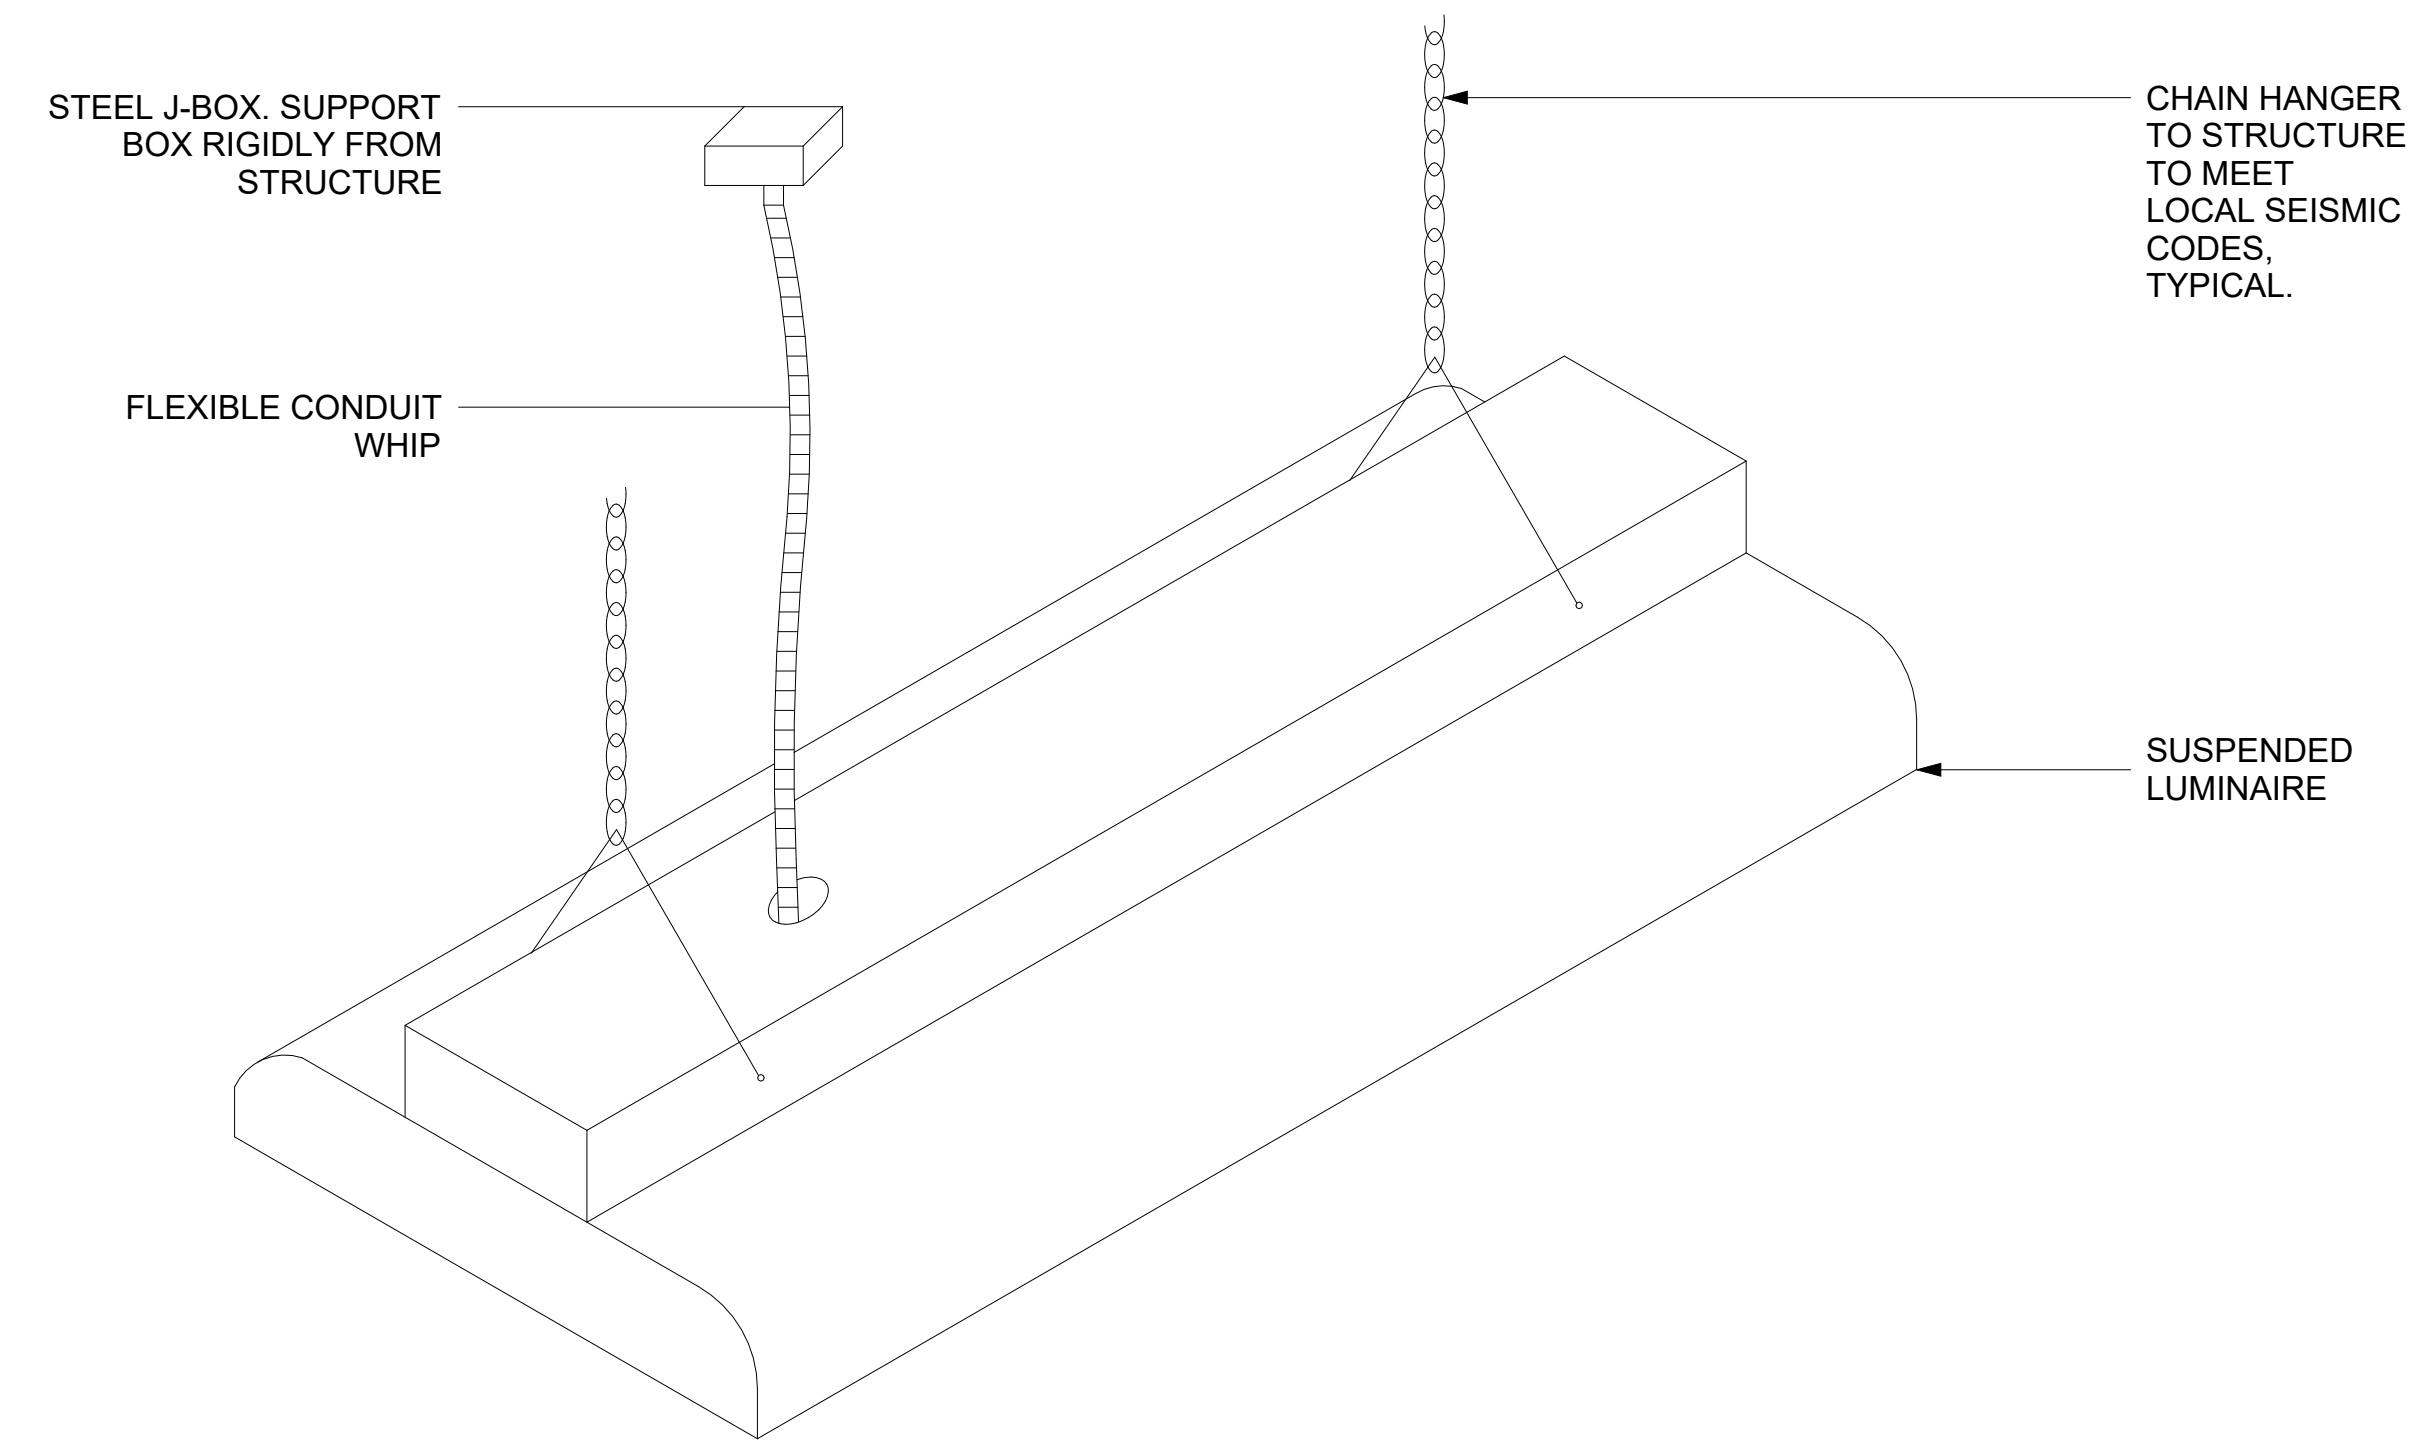

1 TYPICAL SUSPENDED LUMINAIRE INSTALLATION


		CONSULTANT/ DISCIPLINE	ARCHITECT/ ENGINEER OF RECORD	STAMP	Office of Construction and Facilities Management	Drawing Title ELECTRICAL DETAILS	Phase 100% CONSTRUCTION DOCUMENTS	Project Title REPAIR AND WEATHERIZE PARKING STRUCTURE 211 ELEVATOR	Project Number 662-23-111
		<u>DISCIPLINE:</u>	<u>A/E:</u> SPEES DESIGN BUILD 23830 PACIFIC HIGHWAY S. SUITE 300 KENT, WA 98032		 U.S. Department of Veterans Affairs	Approved:	FULLY SPRINKLERED	Location SAN FRANCISCO VA MEDICAL CENTER - SAN FRANCISCO, CA	Building Number 211
								Issue Date 11/17/2025	Drawing Number E-501
		Revisions:	Date:					Checked DCW	Drawn JFO/ONI

GENERAL NOTES

1.
- CONTRACTOR SHALL FIELD VERIFY ALL EXISTING CONDITIONS AS IT PERTAINS TO SUBJECT PROJECT. ANY DISCREPANCIES FOUND SHALL BE REPORTED TO THE ENGINEER.
2.
- CONTRACTOR SHALL PROVIDE ALL SHUTDOWN PLANS, TEMPORARY POWER PLANS, AND PHASING PLANS FOR VA REVIEW AND APPROVAL PRIOR TO COMMENCING WORK. ALL PLANS SHALL BE SUBMITTED FOR REVIEW 30 DAYS PRIOR TO IMPLEMENTATION.
3.
- NOT ALL ONE-LINE DIAGRAM DRAWING SHEETS MAY HAVE WORK SHOWN; ALL ONE-LINE DRAWINGS HAVE BEEN INCLUDED IN THIS DRAWING SET FOR REFERENCE PURPOSES.

KEY NOTES

- 1
- PANELBOARD CONTAINING LIGHTING CIRCUIT TO BE MODIFIED. CONTRACTOR SHALL PERFORM CIRCUIT TRACING TO IDENTIFY EXACT CIRCUIT TO BE MODIFIED. REFERENCE SHEET E-104 FOR ADDITIONAL INFORMATION. CONTRACTOR SHALL UPDATE CIRCUIT DIRECTORY AS APPLICABLE. CIRCUIT DIRECTORY SHALL BE PRINTED AND NOT HANDWRITTEN.
- 2
- PANELBOARD CONTAINING RECEPTACLE CIRCUIT TO BE MODIFIED. CONTRACTOR SHALL PERFORM CIRCUIT TRACING TO IDENTIFY EXACT CIRCUIT TO BE MODIFIED. REFERENCE SHEET E-104 FOR ADDITIONAL INFORMATION. CONTRACTOR SHALL UPDATE CIRCUIT DIRECTORY AS APPLICABLE. CIRCUIT DIRECTORY SHALL BE PRINTED AND NOT HANDWRITTEN.

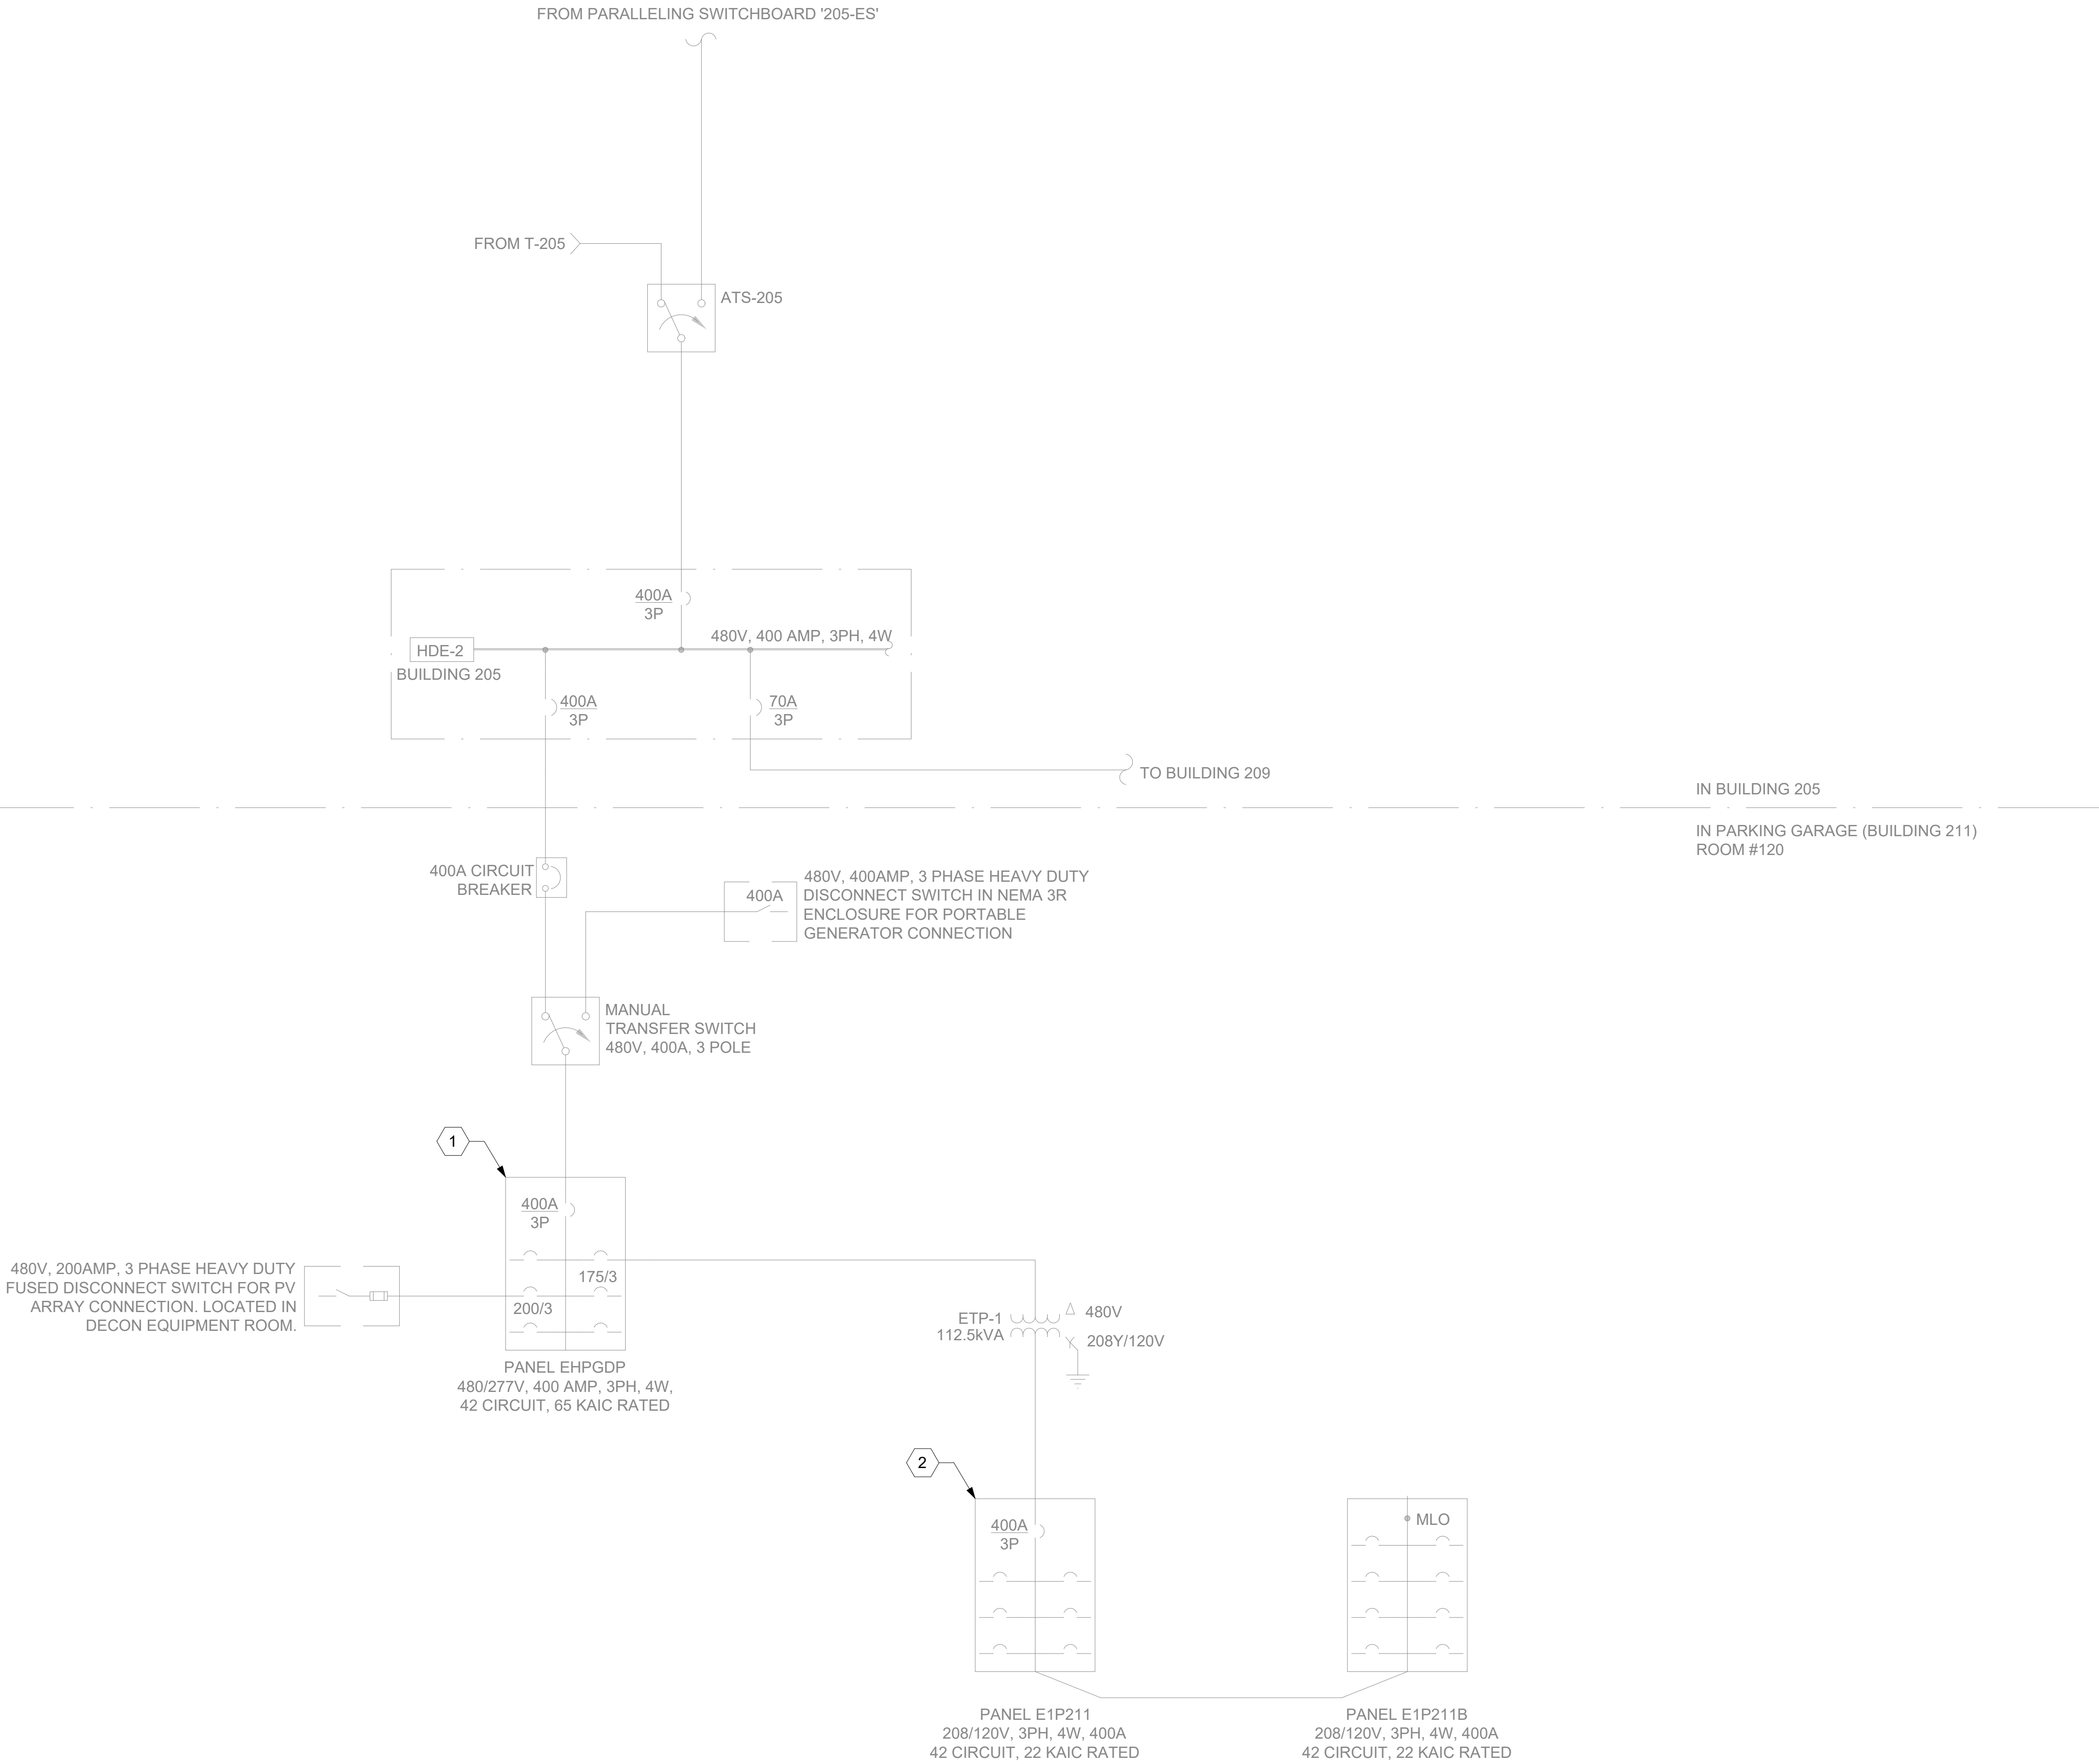

1 ONE-LINE DIAGRAM
NTS

		CONSULTANT/ DISCIPLINE	ARCHITECT/ ENGINEER OF RECORD	STAMP	Office of Construction and Facilities Management	Drawing Title	Phase	Project Title	Project Number	
		DISCIPLINE:	A/E: SPEES DESIGN BUILD 23830 PACIFIC HIGHWAY S. SUITE 300 KENT, WA 98032			ONE-LINE DIAGRAM	100% CONSTRUCTION DOCUMENTS	REPAIR AND WEATHERIZE PARKING STRUCTURE 211 ELEVATOR	662-23-111	
						Approved:	FULLY SPRINKLERED	Location SAN FRANCISCO VA MEDICAL CENTER - SAN FRANCISCO, CA	Building Number 211	
								Issue Date 11/17/2025	Checked DCW	Drawn JFO/ONI
Revisions:	Date:				U.S. Department of Veterans Affairs				E-601	

LUMINAIRE SCHEDULE											
TYPE	DESCRIPTION	LUMENS / COLOR TEMP	DRIVER	WATTS	VOLTS	MOUNTING	MFR	CATALOG #	LENS/DIFFUSER	FINISH	COMMENTS
L1	4' STRIP, SUSPENDED, LED	5729 / 4000K	ELECTRONIC, 0-10V	45.67	120/277V	SUSPENDED, 9'-6" AFF	LITHONIA, OR APPROVED EQUAL	CSS L48 AL03 (5000) UVOLT SSW3 (50) 80CRI	FROSTED	WHITE	-
L2	4' STRIP, SUSPENDED, LED, INTEGRAL OCCUPANCY SENSOR	3735 / 4000K	ELECTRONIC, 0-10V	27.25	120/277V	SUSPENDED, 9'-6" AFF	LITHONIA, OR APPROVED EQUAL	CSS L48 AL03 (3000) MVOLT SSW3 (35) 80CRI	FROSTED	WHITE	-
L3	WALL PACK, LED	5903 / 4000K	ELECTRONIC	47.1	120/277V	WALL, 9'-6" AFF	PHILLIPS GARDCO, OR APPROVED EQUAL	121-16L-530-NW-G4	FROSTED HIGH-IMPACT DIFFUSER	DARK GRAY	PROVIDE WITH INTEGRAL PHOTOCELL, CONTRACTOR SHALL VERIFY COLOR TEMP TO MATCH EXISTING EXTERIOR LIGHTING.
GENERAL NOTES: 1. PRIOR TO LUMINAIRE PROCUREMENT, CONTRACTOR SHALL PROVIDE LIGHTING LAYOUT WITH PROPOSED LUMINAIRES AND INDICATE POINT-BY-POINT PHOTOMETRICS FOR ENGINEER REVIEW DURING SUBMITTAL REVIEW PROCESS.											

PANELBOARD: "EHPGDP" (NOTE 1)													
Location: ELEC 120 Supply From: 205-MZEHS1 VIA 400A MTS Mounting: Surface Enclosure: Type 1				Volts: 480/277V Phases: 3 Wires: 4				A/C Rating: - Bus Rating: 400 A Main Circuit Breaker: 400 A / 3P					
CKT	CIRCUIT DESCRIPTION	Trip	Poles	VA PER PHASE						Poles	Trip	CIRCUIT DESCRIPTION	CKT
				A		B		C					
1	SURGE PROTECTION	30 A	3	100	6235	100	6235	100	6235	3	30 A	ELEVATOR	2
3		*	*							*	*		4
5		*	*							*	*		6
7	TRAILER-35	100 A	3	22170	0	22170	0	22170	0	*	*	SPACE	8
9		*	*							*	*		10
11		*	*							*	*		12
13	CCSE RADIO TRAILER	60 A	3	13302	18226	13302	21832	13302	21832	3	175 A	211-G30 TRANSFORMER FED FROM EHPGDP	14
15		*	*							*	*		16
17		*	*							*	*		18
19	PORTABLE MORGUE - FUTURE USE	40 A	3	0	8314	0	8314	0	8314	3	40 A	EG-7 FAN COIL UNIT	20
21		*	*							*	*		22
23		*	*							*	*		24
25	EDC LIGHTING	20 A	1	1500	1500					1	20 A	GND AND 1ST LIGHTING	26
27	EDC LIGHTING AND WAITING AREA	20 A	1		1500	1500				1	20 A	GND AND 1ST LIGHTING	28
29	SPARE	20 A	1			0	1500	1	1500	1	20 A	GND AND 1ST LIGHTING	30
31	LIGHTING (NOTE 2) (NOTE 3)	20 A	1	1732	1500					1	20 A	LIGHT POLE	32
33	LIGHTING	20 A	1		1500	1500				1	20 A	LIGHT POLE	34
35	LIGHTING	20 A	1			1500	1500			1	20 A	LIGHT POLE	36
37	SPARE	20 A	1	0	4432					1	20 A	UNKNOWN LOAD	38
39	SPARE	20 A	1		0	4432				1	20 A	UNKNOWN LOAD	40
41	SPARE	20 A	1			0	0			1	20 A	SPARE	42
43	RR00M 106, 101	20 A	1	4432	4432					1	20 A	UNKNOWN LOAD	44
45	EDC	20 A	1		4432	1500				1	20 A	STAIRWELLS	46
47	ELECTRICAL CLOSET LIGHTS	20 A	1			1500	1500			1	20 A	ROOF 1-3 POLE LIGHT	48
Total Load:				87855		88318		75118					
Total Amps:				317		519		271					
LOAD TYPE				Connected Load (VA)		Demand Factor		Estimated Demand (VA)		PANEL TOTALS			
Largest Motor				24942		125.00%		31177		Total Conn. Power Load:		251320 VA	
Other				187867		100.00%		187867		Total Est. Power Demand:		259224 VA	
Receptacle				17280		NOTE 4		13640		Total Conn. Amperage:		302 A	
Lighting				21232		125.00%		26540		Total Est. Amperage Demand:		332 A	
Notes: 1. PANELBOARD HAS BEEN AS-BUILT BASED ON CIRCUIT DIRECTORY. 2. CIRCUIT CONTAINING LUMINAIRE FIXTURE TO BE REPLACED. CIRCUIT SHALL BE EXTENDED TO PROVIDED LIGHT FIXTURES. CONTRACTOR SHALL PERFORM CIRCUIT TRACING TO VERIFY CIRCUIT TO BE MODIFIED. CONTRACTOR SHALL UPDATE CIRCUIT DIRECTORY AS APPLICABLE. CIRCUIT DIRECTORY SHALL BE PRINTED AND NOT HANDWRITTEN. 3. TOTAL ADDED LOAD FROM LUMINAIRE FIXTURES IS 161 VA. 4. DEMAND FACTOR OF 50% IS APPLIED AFTER THE FIRST 100VA PER NEC 220.47.													

PANELBOARD: "E1P211" (NOTE 1)											
Location: ELEC 120 Supply From: PNL EHPGDP VIA XFMR ETP-1 Mounting: Surface Enclosure: Type 1				Volts: 208/120V Phases: 3 Wires: 1				A/C Rating: - Bus Rating: 400 A Main Circuit Breaker: 400 A / 3P			
CKT	CIRCUIT DESCRIPTION	Trip	Poles	VA PER PHASE			Poles	Trip	CIRCUIT DESCRIPTION	CKT	
				A	B	C					
1	FACP	20 A	1	500	1080		1	20A	RECEIPT BREAK ROOM AND LOGISTICS	2	
3	REFRIGERATOR	20 A	1		1920	1080		1	20 A	RECEIPT OPERATIONS AND LOGISTICS	4
5	MICROWAVE	20 A	1			1920	1080	1	20 A	RECEIPT OPERATIONS AND LOGISTICS	6
7	COPIER	30 A	2	2400	1080			1	20 A	RECEIPT EDC AREA	8
9		*	*		2400	1080		1	20 A	RECEIPT EDC AREA AND AVV NOOK	10
11	COMM EQUIPMENT	20 A	1			1920	1080	1	20 A	RECEIPT AVV NOOK	12
13	COMM EQUIPMENT	20 A	1	1920	1080			1	20 A	RECEIPT EDC PLUG STRIP	14
15	EF 4-S	20 A	1		1920	1080		1	20 A	RECEIPT EDC PLUG STRIP	16
17	RECEIPT IN WAITING, MECH. & WC (NOTE 2)	20 A	1			1080	1080	1	20 A	RECEIPT OFFICES	18
19	RECEIPT IN WAITING AND JANITORS CLOSET	20 A	1	1080	1080			1	20 A	RECEIPT OFFICES	20
21	RECEIPT IN STORAGE AREAS	20 A	1		1050	2400		2	30 A	SERVER DATA SWITCH	22
23	RECEIPT STORAGE AREA	20 A	1			1080	2400	1	20 A		24
25	RECEIPT STORAGE AREA	20 A	1	1050	1920			1	20 A	LCP POWER	26
27	WC/JANITOR LIGHTS EF 1,2,3	20 A	1		1500	1920		1	20 A	LCP POWER	28
29	SPARE	20 A	1			0	1920	1	20 A	LCP POWER	30
31	RECEIPT GARAGE ELEVATOR	20 A	1	1050	1920			1	20 A	LCP POWER	32
33	SECURITY ACCESS PANEL	20 A	1		1000	1920		1	20 A	LCP POWER	34
35	SPARE	20 A	1			0	1920	1	20 A	LCP POWER	36
37	SPARE	30 A	3	0	1920			1	20 A	LCP POWER	38
39		*	*		0	1920		1	20 A	LCP POWER	40
41		*	*			0	1920	1	20 A	ELEVATOR GAS LIGHTS AND FAN	42
Total Load				8520	21832	17485					
Total Amps				352	102	145					
PANEL TOTALS											
LOAD TYPE		Connected Load (VA)		Demand Factor		Estimated Demand (VA)					
Largest Motor		4992		125.00%		6340		Total Conn. Power Load		57564 VA	
Other		35292		100.00%		35292		Total Est. Power Demand		55172 VA	
Receptacle		17280		NOTE 3		13640		Total Conn. Amperage:		160 A	
Lighting		0		125.00%		0		Total Est. Amperage Demand:		153 A	
Notes:											
1. PANELBOARD HAS BEEN AS-BUILT BASED ON CIRCUIT DIRECTORY. NO LOAD ADDED TO PANELBOARD.											
2. CIRCUIT CONTAINING RECEPTACLE TO BE REPLACED. CONTRACTOR SHALL VERIFY CIRCUIT TRACING TO CONFIRM CIRCUIT TO BE MODIFIED. CONTRACTOR SHALL UPDATE CIRCUIT DIRECTORY AS APPLICABLE. CIRCUIT DIRECTORY SHALL BE PRINTED AND NOT HANDWRITTEN.											
3. DEMAND FACTOR OF 50% IS APPLIED AFTER THE FIRST 100VA PER NEC 220.47.											

--	--	