


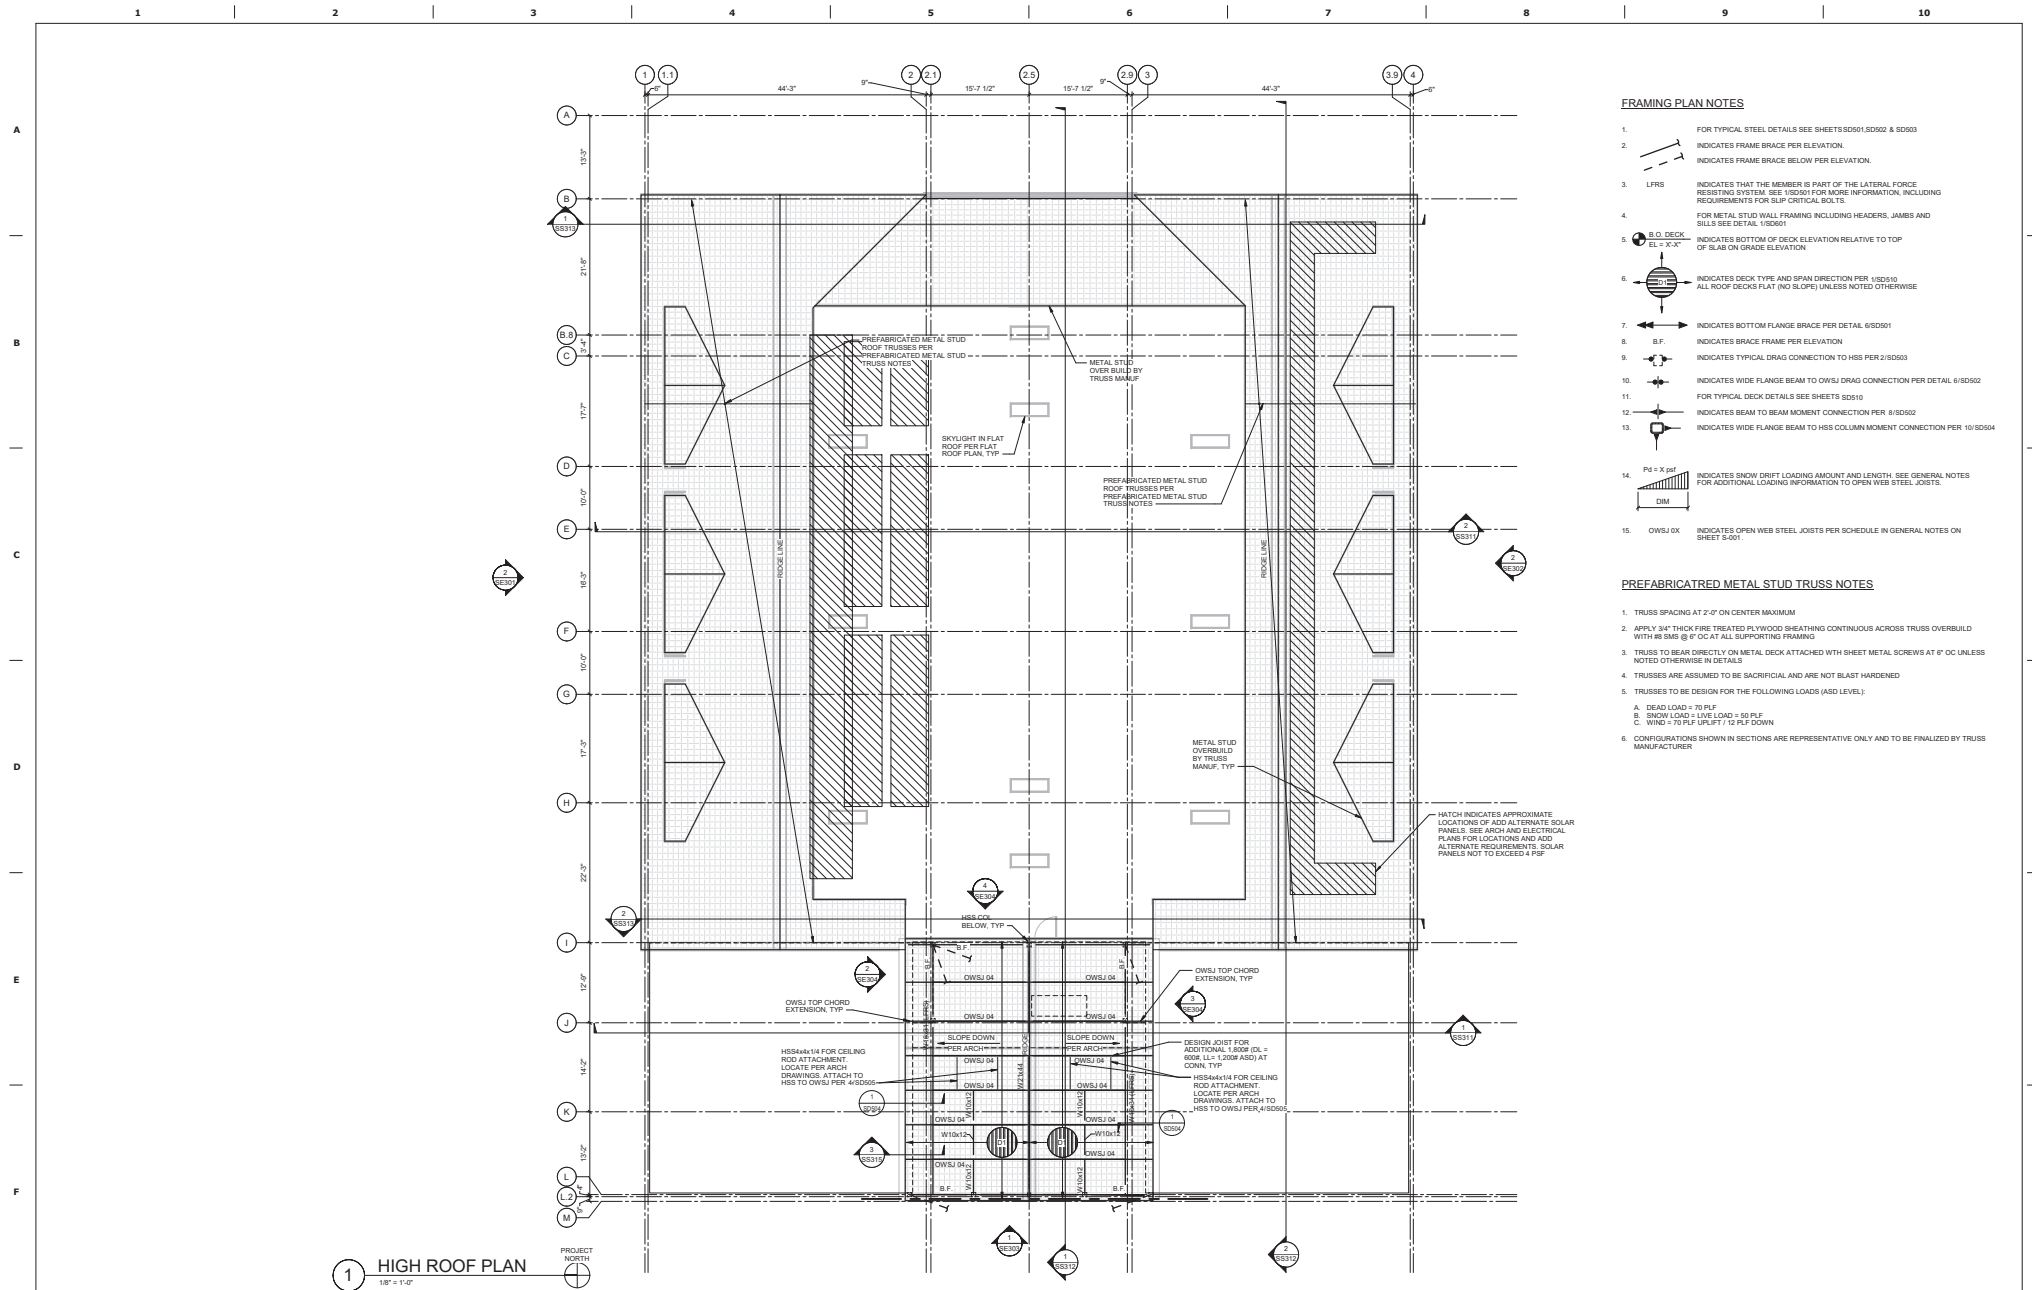

FRAMING PLAN NOTES


- FOR TYPICAL STEEL DETAILS SEE SHEETS SD001, SD002 & SD003
- INDICATES FRAME BRACE PER ELEVATION.
- LFRS INDICATES THAT THE MEMBER IS PART OF THE LATERAL FORCE RESISTING SYSTEM. SEE 150009 FOR MORE INFORMATION, INCLUDING REQUIREMENTS FOR SLIP CRITICAL BOLTS.
- FOR METAL STUD WALL FRAMING INCLUDING HEADERS, JAMBS AND SILL SEE DETAIL 150001
- INDICATES BOTTOM OF DECK ELEVATION RELATIVE TO TOP OF SLAB ON GRADE ELEVATION
- INDICATES DECK TYPE AND SPAN DIRECTION PER 150010
ALL ROOF DECKS FLAT (NO SLOPE) UNLESS NOTED OTHERWISE
- INDICATES BOTTOM FLANGE BRACE PER DETAIL 6/SD001
- B.F. INDICATES BRACE FRAME PER ELEVATION
- INDICATES TYPICAL DRAG CONNECTION TO HSS PER 2/SD003
- INDICATES WIDE FLANGE BEAM TO OWSJ DRAG CONNECTION PER DETAIL 6/SD002
- FOR TYPICAL DECK DETAILS SEE SHEETS SD010
- INDICATES BEAM TO BEAM MOMENT CONNECTION PER 8/SD002
- INDICATES WIDE FLANGE BEAM TO HSS COLUMN MOMENT CONNECTION PER 10/SD004
- INDICATES SNOW DRIFT LOADING AMOUNT AND LENGTH. SEE GENERAL NOTES FOR ADDITIONAL LOADING INFORMATION TO OPEN WEB STEEL JOISTS.
- OWSJ OX INDICATES OPEN WEB STEEL JOISTS PER SCHEDULE IN GENERAL NOTES ON SHEET S-001.

PREFABRICATED METAL STUD TRUSS NOTES

- TRUSSES SPACING AT 2'-0" ON CENTER MAXIMUM
- APPLY 3/4" THICK FIRE TREATED PLYWOOD SHEATHING CONTINUOUS ACROSS TRUSS OVERBUILD WITH 8# SMS @ 6" OC AT ALL SUPPORTING FRAMING
- TRUSSES TO BEAR DIRECTLY ON METAL DECK ATTACHED WITH SHEET METAL SCREWS AT 6" OC UNLESS NOTED OTHERWISE IN DETAILS
- TRUSSES ARE ASSUMED TO BE SACRIFICIAL AND ARE NOT BLAST HARDENED
- TRUSSES TO BE DESIGN FOR THE FOLLOWING LOADS (ASD LEVEL):
A. DEAD LOAD = 70 PLF
B. SNOW LOAD = LIVE LOAD = 50 PLF
C. WIND = 70 PLF UPLIFT / 10 PLF DOWN
- CONFIGURATIONS SHOWN IN SECTIONS ARE REPRESENTATIVE ONLY AND TO BE FINALIZED BY TRUSS MANUFACTURER

1 HIGH ROOF PLAN

1/8" = 1'-0"

 		CONSULTANT		ARCHITECT/ENGINEER OF RECORD		STAMP		Office of Construction and Facilities Management		Drawing Title HIGH ROOF PLAN		Phase CONSTRUCTION DOCUMENTS		Project Title CONSTRUCT PRIMARY CARE / MENTAL HEALTH BUILDING		Project Number 531-325					
		kpff 412 E. Park Center Blvd, Suite 200 Boise, ID 83706 O: 208.316.6985 www.kpff.com		A/E: SPEES DESIGN BUILD 625 1ST AVE #301 SEATTLE, WA, 98014 (360) 223 - 8994 RAY SPEES, PRESIDENT  SPEES DESIGN BUILD				VA U.S. Department of Veterans Affairs		Approved: MEDICAL CENTER DIRECTOR								Building Number 127			
										Approved: CHIEF, FACILITY MANAGEMENT SERVICE				Location BOISE VA MEDICAL CENTER - BOISE, ID		Drawing Number SF203					
Revisions:		Date:												Issue Date 07/23/2021		Checked CH/JW		Drawn SG		029 OF 206	