


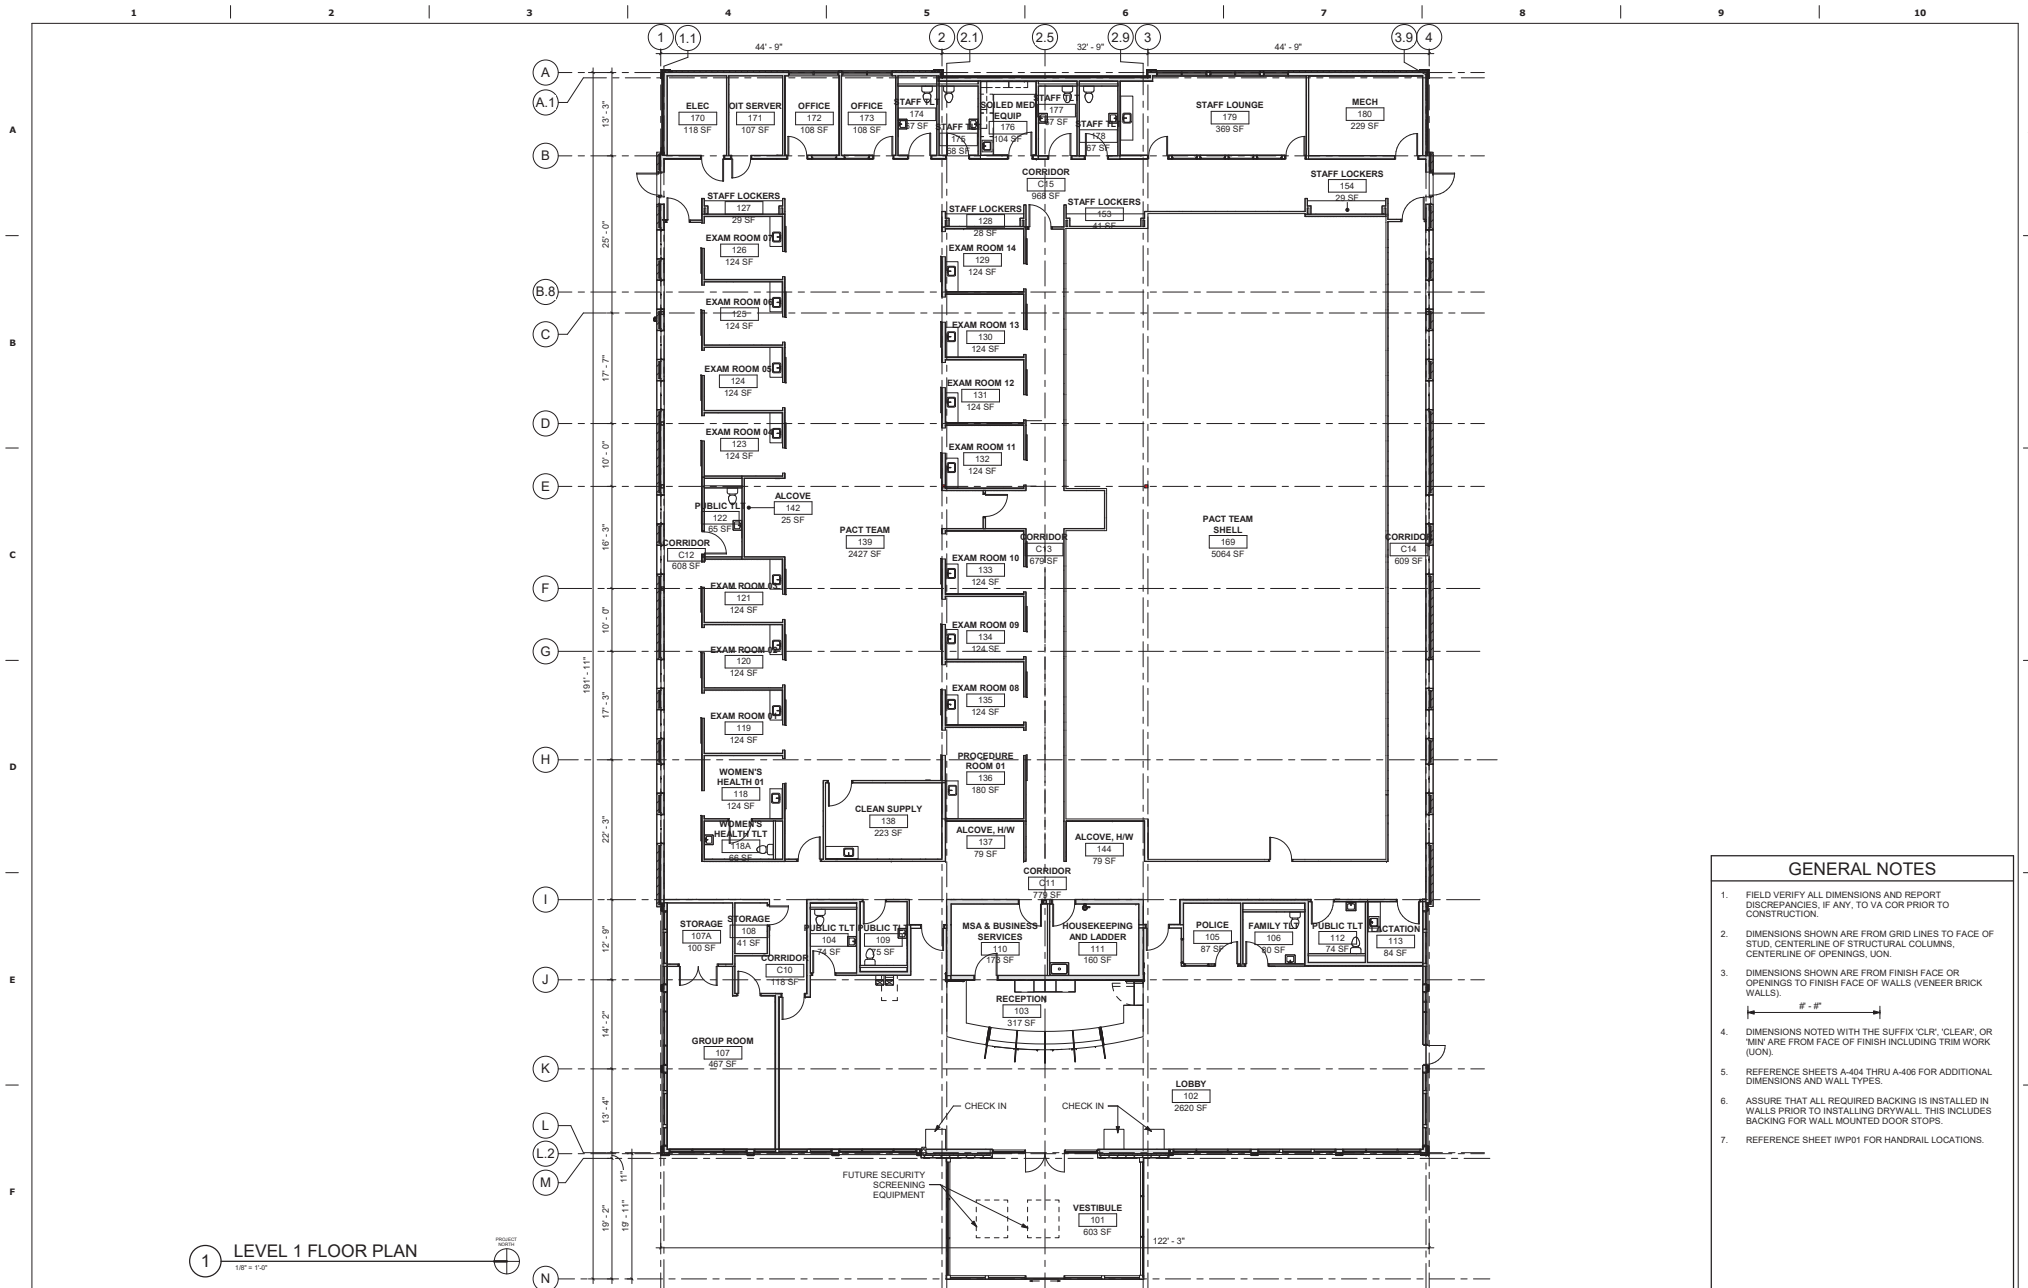

Revisions:	Date:

CONSULTANT

ARCHITECT/ENGINEER OF RECORD
A/E: SPEES DESIGN BUILD 625 1ST AVE #301 SEATTLE, WA, 98014 (206) 590-2118 RAY SPEES, PRESIDENT

STAMP
10000 REGISTERED ARCHITECT STATE OF WASHINGTON

Office of Construction and Facilities Management
VA U.S. Department of Veterans Affairs

Drawing Title
FLOOR PLAN
Approved: MEDICAL CENTER DIRECTOR
Approved: CHIEF, FACILITY MANAGEMENT SERVICE

Phase
CONSTRUCTION DOCUMENTS

Project Title
CONSTRUCT PRIMARY CARE / MENTAL HEALTH BUILDING
Location
BOISE VA MEDICAL CENTER - BOISE, ID
Issue Date
07/23/2021
Checked
MK
Drawn
MA
Project Number
531-325
Building Number
127
Drawing Number
A-101
052 OF 206