

4. RETUR TO ROOM FRESH SCHEDULE FOR SPECIFIC CEILING EXHAUSTIONS

5. ROOM FRESH SCHEDULE IN SPECIFICATIONS SECTION 08 00 00

6. SPRINKLER VALVES AND ALL CEILING MOUNTED ELECTRICAL DEVICES TO BE IDENT OF CEILING PANEL AS SHOWN BY THE PANEL IDENT.


7. RETAIL IN THE CEILING PANEL IDENT. WHERE APPLICABLE

8. HVAC OFFICES SHOWN FOR COORDINATION ONLY - SEE MECHANICAL HVAC PLANS FOR COORDINATION ONLY - SEE ELECTRICAL PLANS FOR COORDINATION ONLY - SEE ELECTRICAL PLANS FOR MORE INFORMATION ON LOADING

9. LIGHTING AND ELECTRICAL DEVICES SHOWN FOR COORDINATION ONLY - SEE ELECTRICAL PLANS FOR MORE INFORMATION ON LOADING

10. EXPOSED STRUCTURE, WHERE OCCURS, IS NOT SHOWN FOR CLARITY

	1" x 4' PENDANT LUMINAIRE
	2' x 2' RECESSED LUMINAIRE
	1' x 4' RECESSED LUMINAIRE
	2' x 4' RECESSED LUMINAIRE
	DECORATIVE PENDANT
	RECESSED CAN LUMINAIRE
	CEILING MOUNTED DOT LIGHT
	1' x 2' RETURN AIR GRILLE
	2' x 2' RETURN AIR GRILLE
	1' x 2' DIFFUSER
	2' x 2' DIFFUSER
	1' x 4' DIFFUSER
	LINEAR SLOT DIFFUSER
	2' x 4' LINEAR FLOW
	1' x 2' EXHAUST
	2' x 2' EXHAUST
	10' x 10' EXHAUST
	ACCESS DOOR/PANEL
	ELEVATION A/F

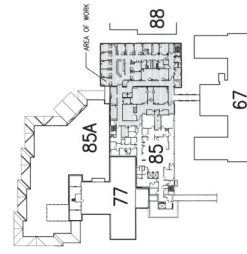[illegible]

THIRD FLOOR KEY PLAN
SCALE: 1/8" = 1'-0"



FOR CONSTRUCTION

AG 3

BUILDING NUMBER	CHECKED	UNPAID
85	ST	

APPROVED: CHIEF OF FACILITY MANAGEMENT SERVICE

85AFL_KEYPLAN.dwg
531-317_xVAbord.dwg

Architects and Planners, Chartered
565 W. Myrtle Street, Suite 225 Boise, Idaho 83702-7606



BUILDING 85 - THIRD FLOOR REFLECTED CEILING PLAN



BUILDING 85

--	--

REDUCT ALTERNATE #5 - SHELL 0.8 SUITE
SAME AS BASE BUT EXCEPT DELETE TANK IMPROVEMENTS AS REQUIRED FOR THE 3RD FLOOR OPENING ROOM SUITE. THIS ALTERNATE WILL INCLUDE LIMITED IMPROVEMENTS TO THE BASE BUILDING TO MAINTAIN THE EXISTING FUNCTIONALITY OF THE BUILDING. MAINTAIN EXISTING BASE BOOM EQUIPMENT SUPPORT STRUCTURES SHOWN ON SHEET 56.1. EXCEPT AS SHOWN ON DRAWINGS E10.3 AND E10.3C. EXCEPT AS SHOWN ON DRAWINGS E10.3 AND E10.3C.

	1" x 4" PINOUT LUMINARE
	2" x 2" RECESSED LUMINARE
	1" x 4" RECESSED LUMINARE
	2" x 4" RECESSED LUMINARE
	DECORATIVE PINOUT
+	
	RECESSED ON LUMINARE
	CEILING MOUNTED EXIT LIGHT
	1" x 2" RETURN AIR GRILLE
	2" x 2" RETURN AIR GRILLE
	1" x 2" DIFFUSER
	2" x 2" DIFFUSER
	1" x 4" DIFFUSER
	1" x 2" FANLIGHT
	2" x 2" FANLIGHT
	10" x 10" FANLIGHT
	ACCESS DOOR/PANEL
	EGRESS DOOR



BUILDING 85 - THIRD FLOOR DEDUCT ALTERNATE REFLECTED CEILING PLAN
NOT TO SCALE

DATE	11/01/2011
PROJECT NO.	531-317
DRAWING NO.	A10.3C

FOR CONSTRUCTION




REPRESENTATIVE OF CONTRACTORS ASSOCIATION

GENERAL SHEET NOTES

- A. FOR GENERAL STRUCTURAL NOTES, ABBREVIATIONS, AND LEGEND SEE DRAWINGS S0.1 AND S0.2.
- B. ALL DIMENSIONS ARE TO THE CENTRINE OF MEMBERS, BACK FACE OF CHANNEL MEMBERS, OR FACE OF WALL.
- C. DIMENSIONS SHOWN TO LOCATE MEDICAL EQUIPMENT SUPPORTS ARE FOR BID PURPOSES ONLY. CONTRACTOR SHALL COORDINATE EQUIPMENT MANUFACTURER FINAL SUPPORTS WITH ARCHITECTURAL PRIOR TO FABRICATION OR INSTALLATION OF SUPPORTS. COORDINATE ALL EQUIPMENT LOCATIONS WITH ARCHITECTURAL.
- D. SEE DWG S6.1 AND S6.3 FOR TYPICAL CEILING MOUNTED EQUIPMENT SUPPORT DETAILS.

SHEET KEYNOTES


1. TRUSS/UP LIGHT AND FLAT PANEL SUPPORT. SEE DETAIL 1 ON DWG S6.2
2. TRUSS/UP EQUIPMENT BOOM SUPPORT. SEE DETAIL 4 ON DWG S6.2
3. DETAIL 3 ON S6.2
4. EQUIPMENT LATERAL BRACE LOCATION. SEE DETAIL 3 ON S6.2
5. CB-115 THREADED ROD HANGER SUPPORT. SEE DETAILS 2 AND 3 ON DWG S6.3
6. FOR EJECT ALTERNATIVE NUMBER 5, OMIT WORK SHOWN

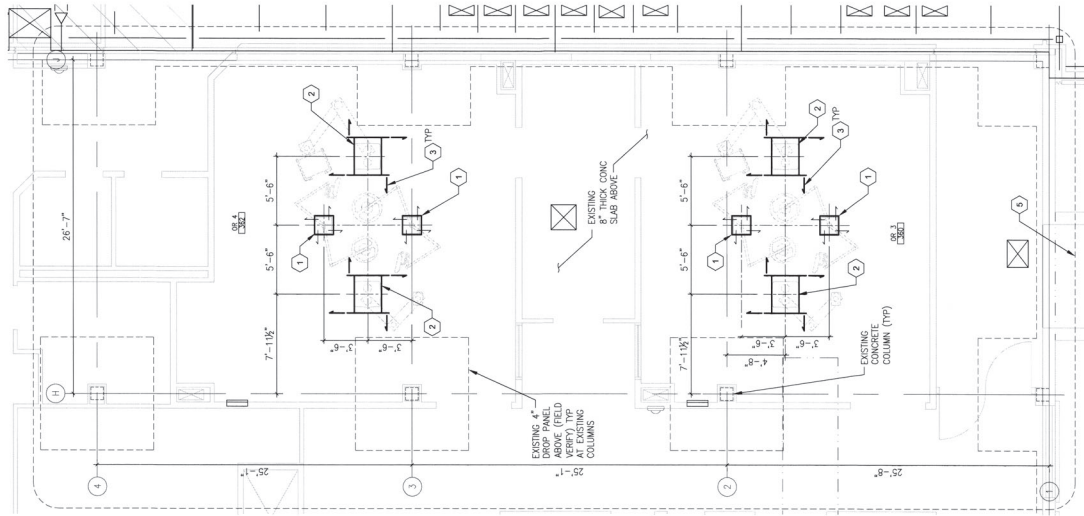

EXISTING MAIN ROOF STRUCTURE ABOVE SHOWN
TOC EL. 138'-8" FIELD VERIFY




THIRD FLOOR CEILING MOUNTED EQUIPMENT PLAN
1/4"=1'-0"

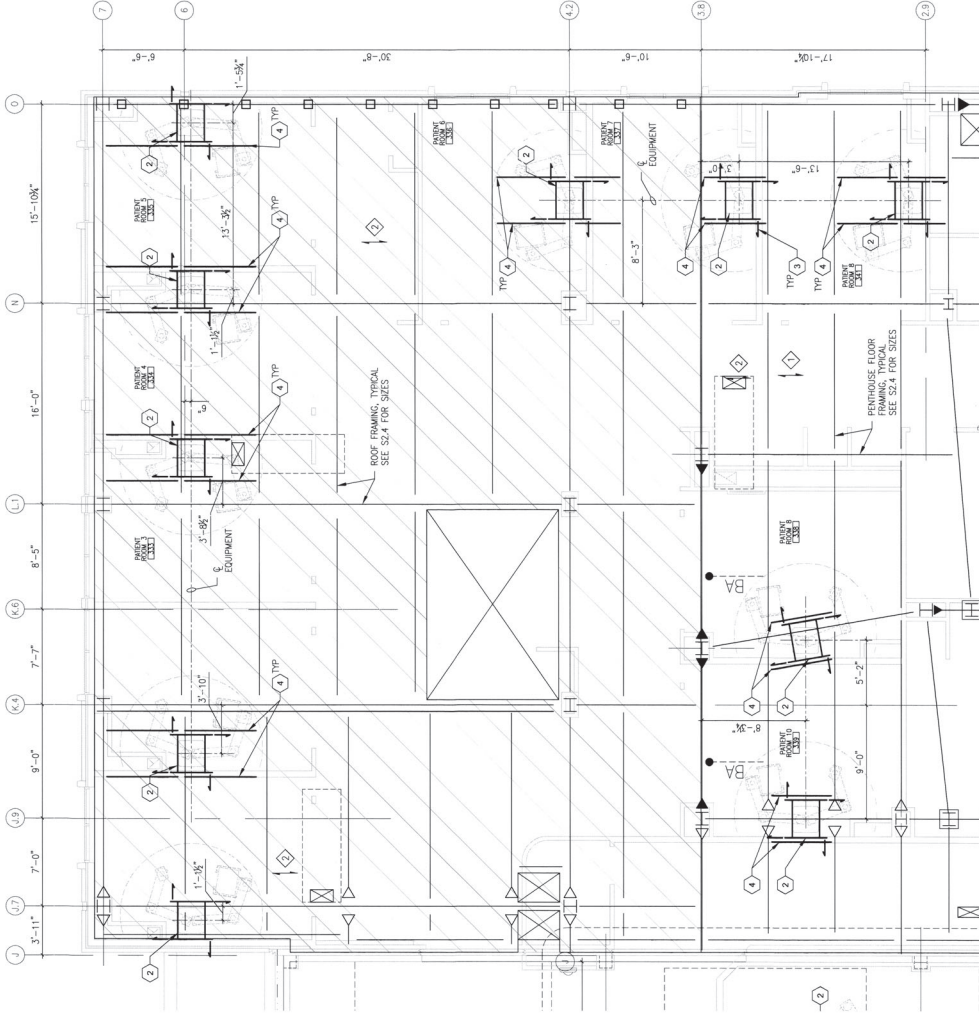

NEW MAIN ROOF/PENTHOUSE FRAMING ABOVE SHOWN
TOC EL. 138'-8"
TOC EL. 138'-4"



THIRD FLOOR CEILING MOUNTED EQUIPMENT PLAN
1/4"=1'-0"

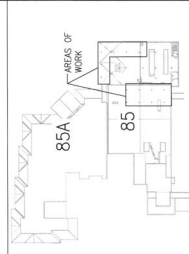

ROOF/PENTHOUSE KEY PLAN
NOT TO SCALE

DATE: 11/01/2011
PROJECT NO.: 531-317
DRAWING NO.: S6.1
SHEET NO.: 75 OF 148

REPLACE AND MODERNIZE SURGERY / INTENSIVE CARE UNIT
BUILDING NUMBER: 85
CHECKED: KES
DESIGNED: LAH
LOCATION: VAMC BOISE, IDAHO

ENLARGED EQUIPMENT SUPPORT PLANS AND DETAILS
APPROVED: CHIEF OF FACILITY MANAGEMENT SERVICE
APPROVED: MEDICAL CENTER DIRECTOR

ARCHITECTS AND PLANNERS, CHARTERED
505 W. MYRTLE STREET, SUITE 225 BOISE, IDAHO 83702-7606

CH2MHILL®
322 EAST FRONT STREET, SUITE 200, BOISE, ID 83702

7747
ARCHITECTS
DATE: 11/01/2011

REVISIONS

