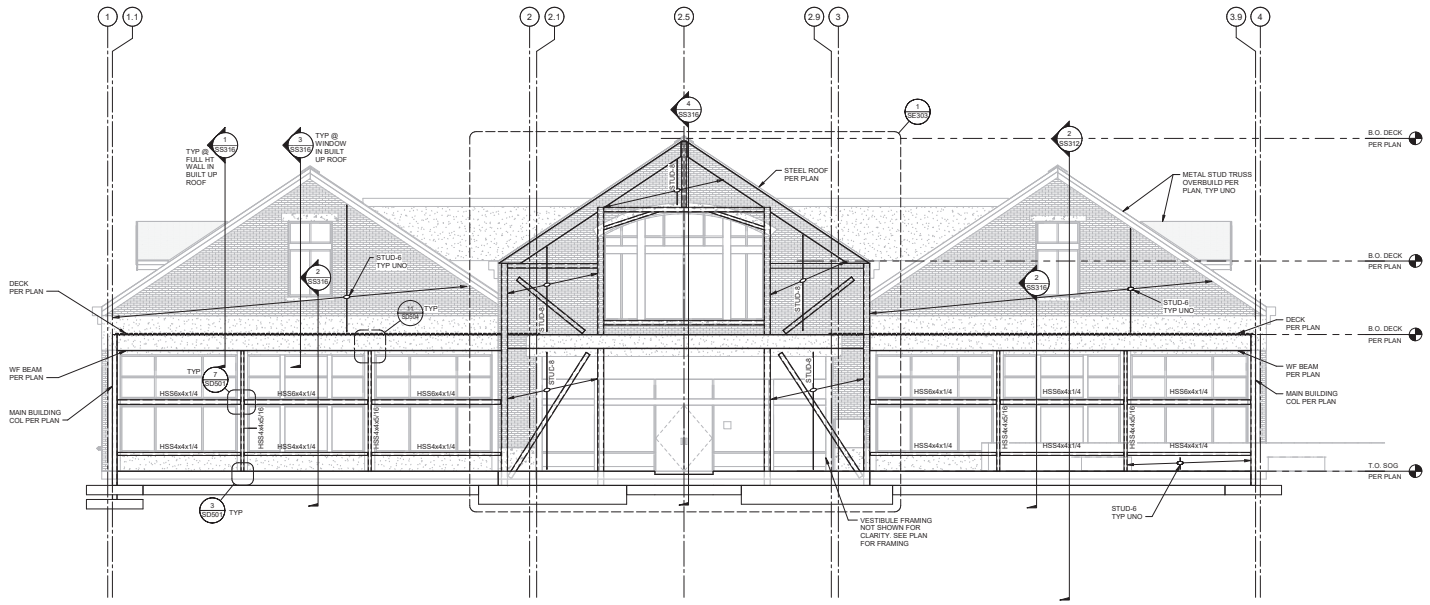

NOTE:
1. STUD-X INDICATES NON-BEARING METAL STUD WALL SIZE AND SPACING PER SCHEDULE IN DETAIL 1/SD601

1 WEST ELEVATION
1/SE301 — 3/16" = 1'-0"

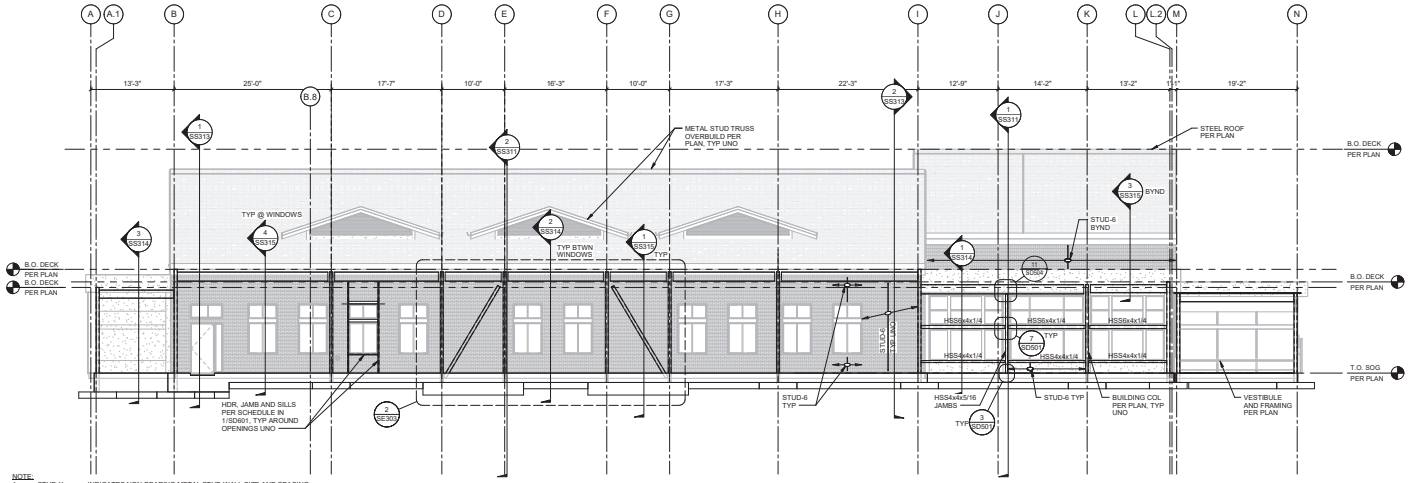

NOTE:
1. STUD-X INDICATES NON-BEARING METAL STUD WALL SIZE AND SPACING PER SCHEDULE IN DETAIL 1/SD601

2 NORTH ELEVATION
2/SE301 — 1/8" = 1'-0"

Revisions:	**Date:**

CONSULTANT
kpff
412 E. Park Center Blvd, Suite 200
Boise, ID 83706
O: 208.336.6985
www.kpff.com

ARCHITECT/ENGINEER OF RECORD
A/E:
SPEES DESIGN BUILD
625 1ST AVE #301
SEATTLE, WA, 98014
(360) 223 - 8994
RAY SPEES, PRESIDENT
SPEESDESIGNBUILD

STAMP
REGISTERED PROFESSIONAL ENGINEER 12033 STATE OF IDAHO JOHN M. BILLAU

Office of Construction and Facilities Management
U.S. Department of Veterans Affairs

Drawing Title BUILDING ELEVATIONS	**Phase** CONSTRUCTION DOCUMENTS	**Project Title** CONSTRUCT PRIMARY CARE / MENTAL HEALTH BUILDING	**Project Number** 531-325
Approved: MEDICAL CENTER DIRECTOR		**Location** BOISE VA MEDICAL CENTER - BOISE, ID	**Building Number** 127
Approved: CHIEF, FACILITY MANAGEMENT SERVICE		**Issue Date** 07/23/2021 / **Checked** CH/JW / **Drawn** SG	**Drawing Number** SE301
			030 OF 206

VA FORM 08 - 6231