


GENERAL NOTES	
1	Keep cable runs as short as possible and not to exceed 300 feet.
2	Follow CIPA requirements
3	Keep Maintenance loops as short as possible.
4	End cable with maintenance loop

REFERENCE	
	4 Port Data Outlet
	2 Port Data Outlet
	IT Closet Location
	Quadplex Outlet
	Quadplex Outlet - Emergency


WORK NEEDED	
DATA CABLE PULLS	16
POWER CABLE PULLS	1

KEY NOTE	
1.	ROUTE 400.1.1P TO 1ST FLOOR ELECTRICAL CLOSET ROOM# 1051A, CIRCUIT NP1-1-24SD

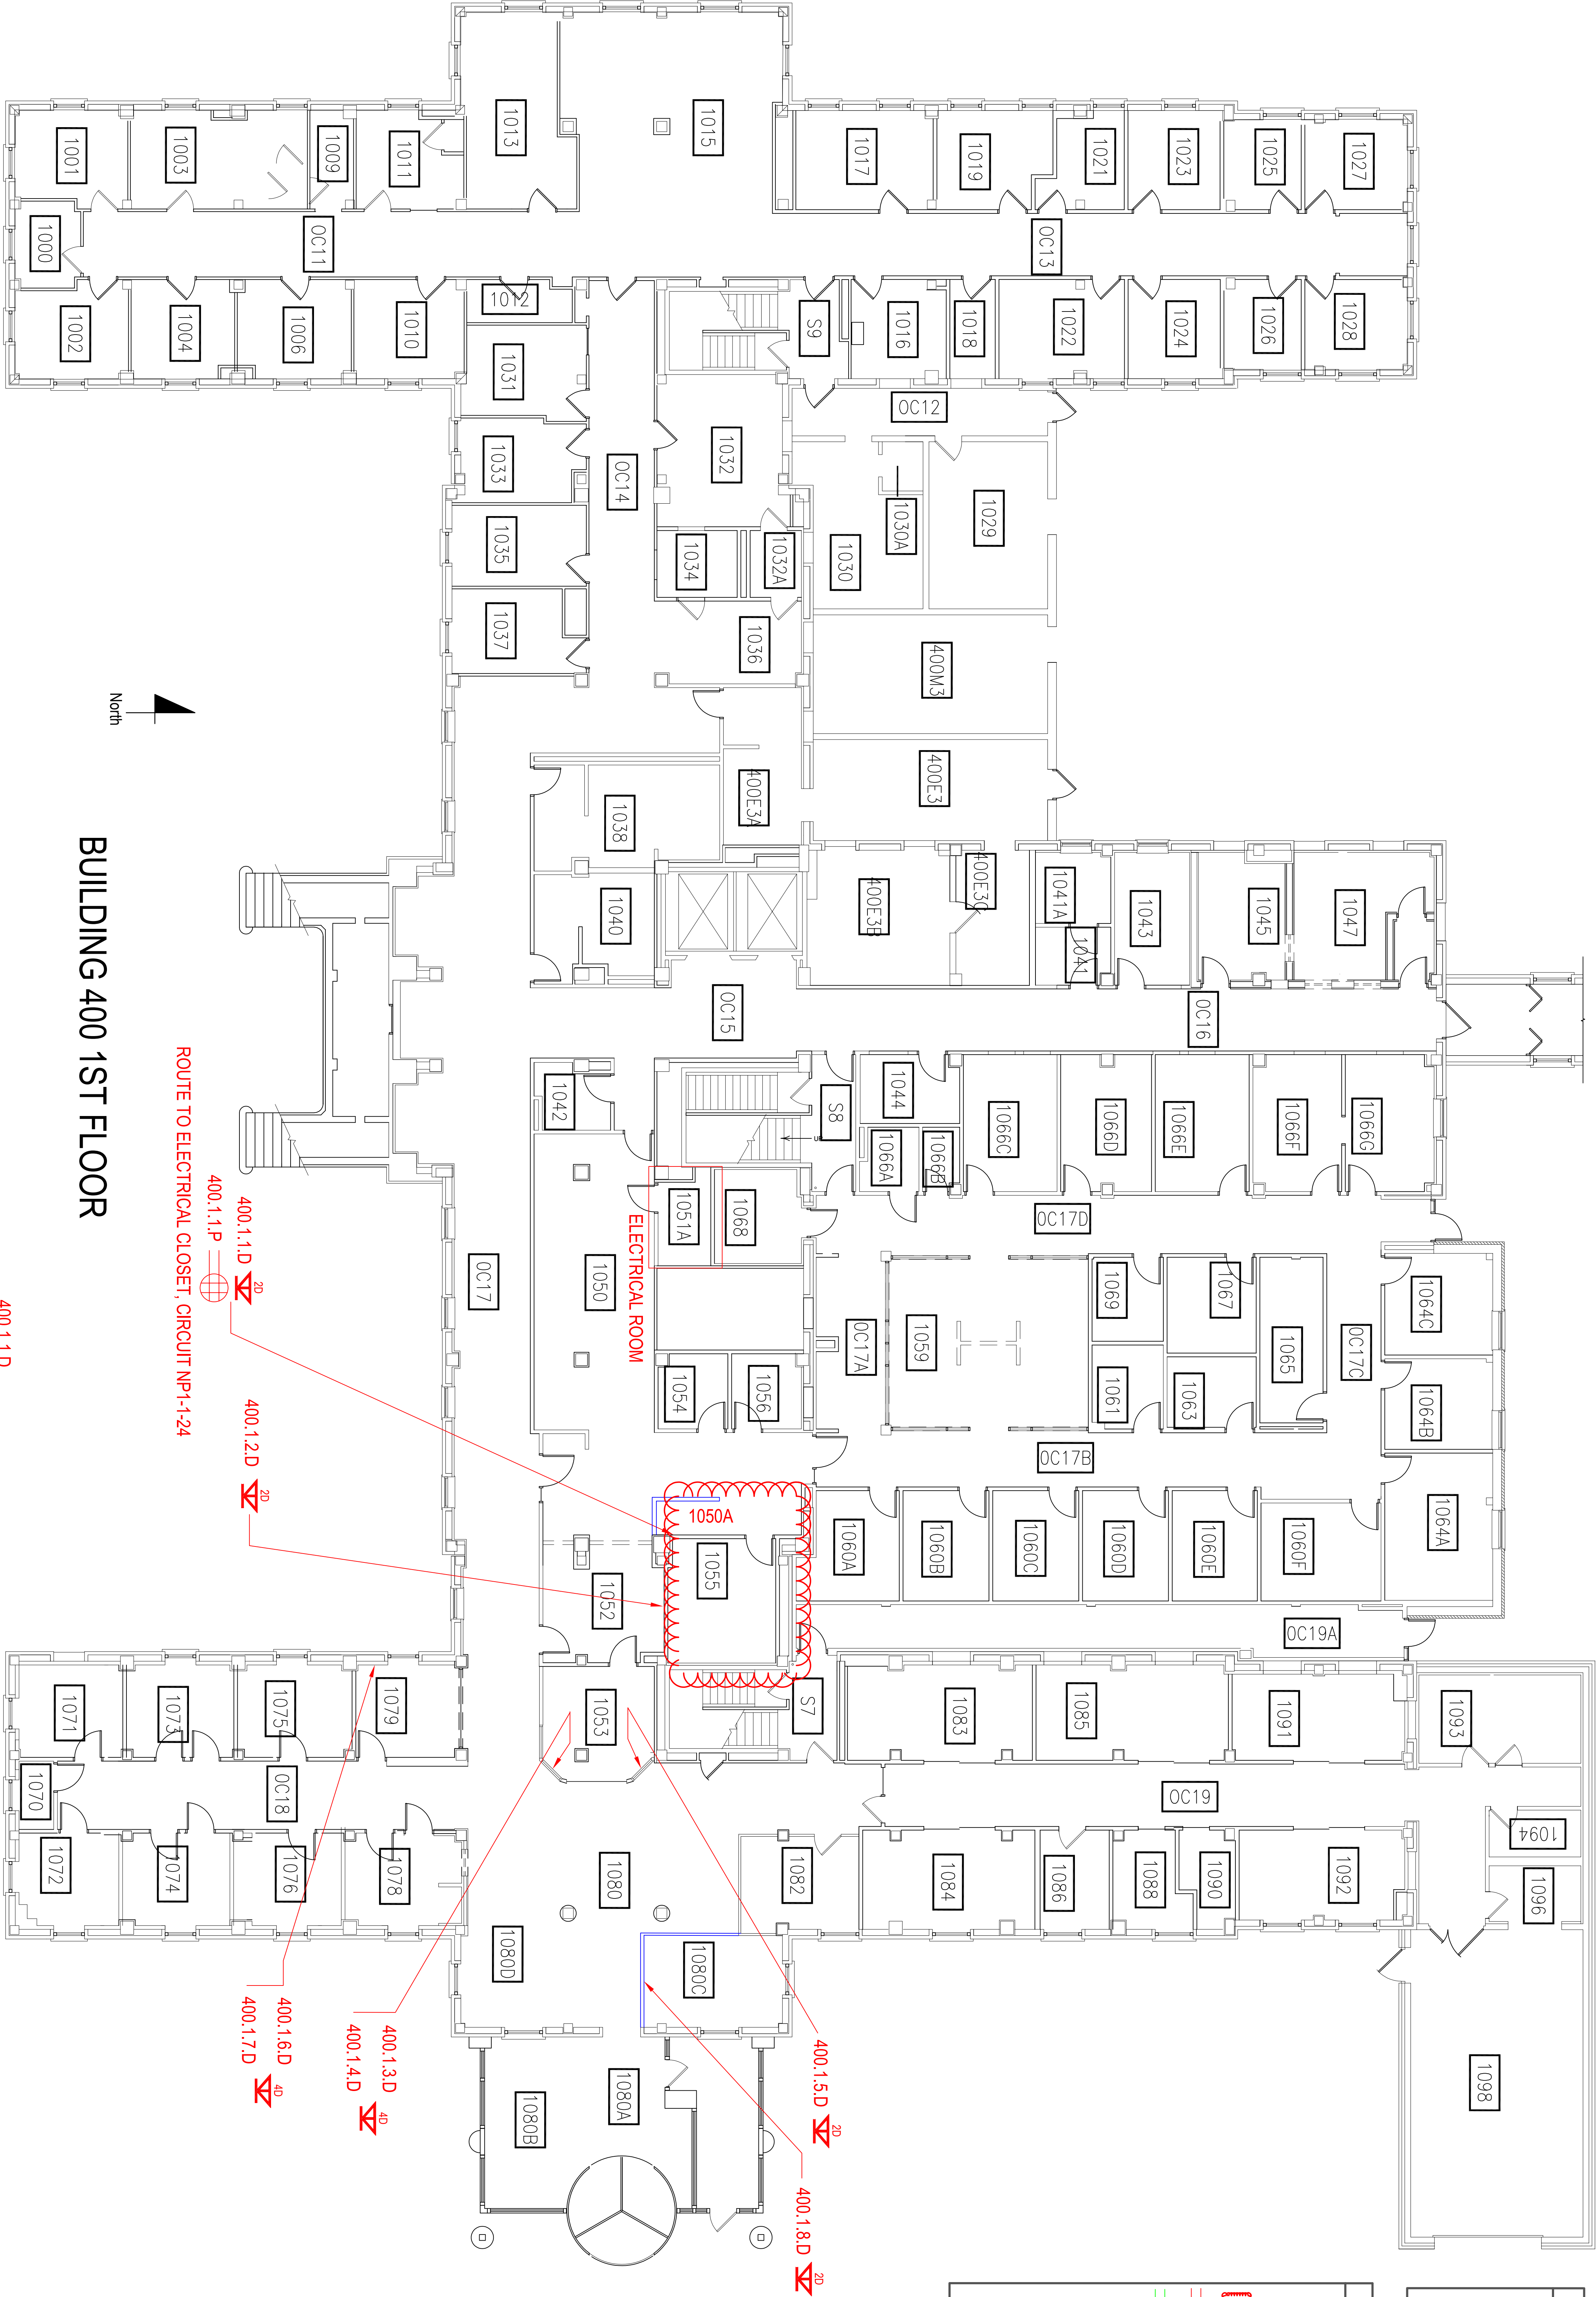

Revisions:

Date	

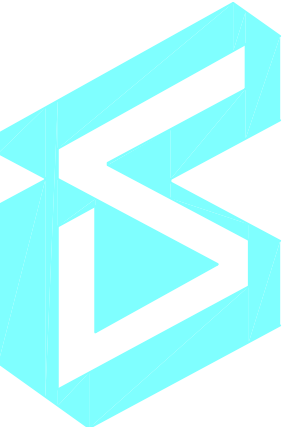


Dept. of Veterans Affairs
Medical Center
500 East Veterans Street
Tomah, WI, 54660




CONSULTANTS:	

Drawing Title		Project Title	
BLD 400 FLOOR 1		DATA DROPS POWER OUTLETS PER CSR DECEMBER 2025	
Approved: Project Director		Location	Tomah, Wisconsin
Date	01-07-2026	Checked By:	JMS
		Drawn By:	
DDPO-400-1		Drawing Number	
		Building Number	400
		Project Number	676-26-702
		Office of Facilities Management	



100% - CONSTRUCTION DOCS

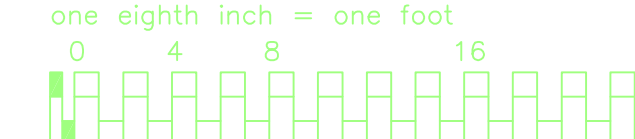

VA FORM 08-6231, OCT 1978

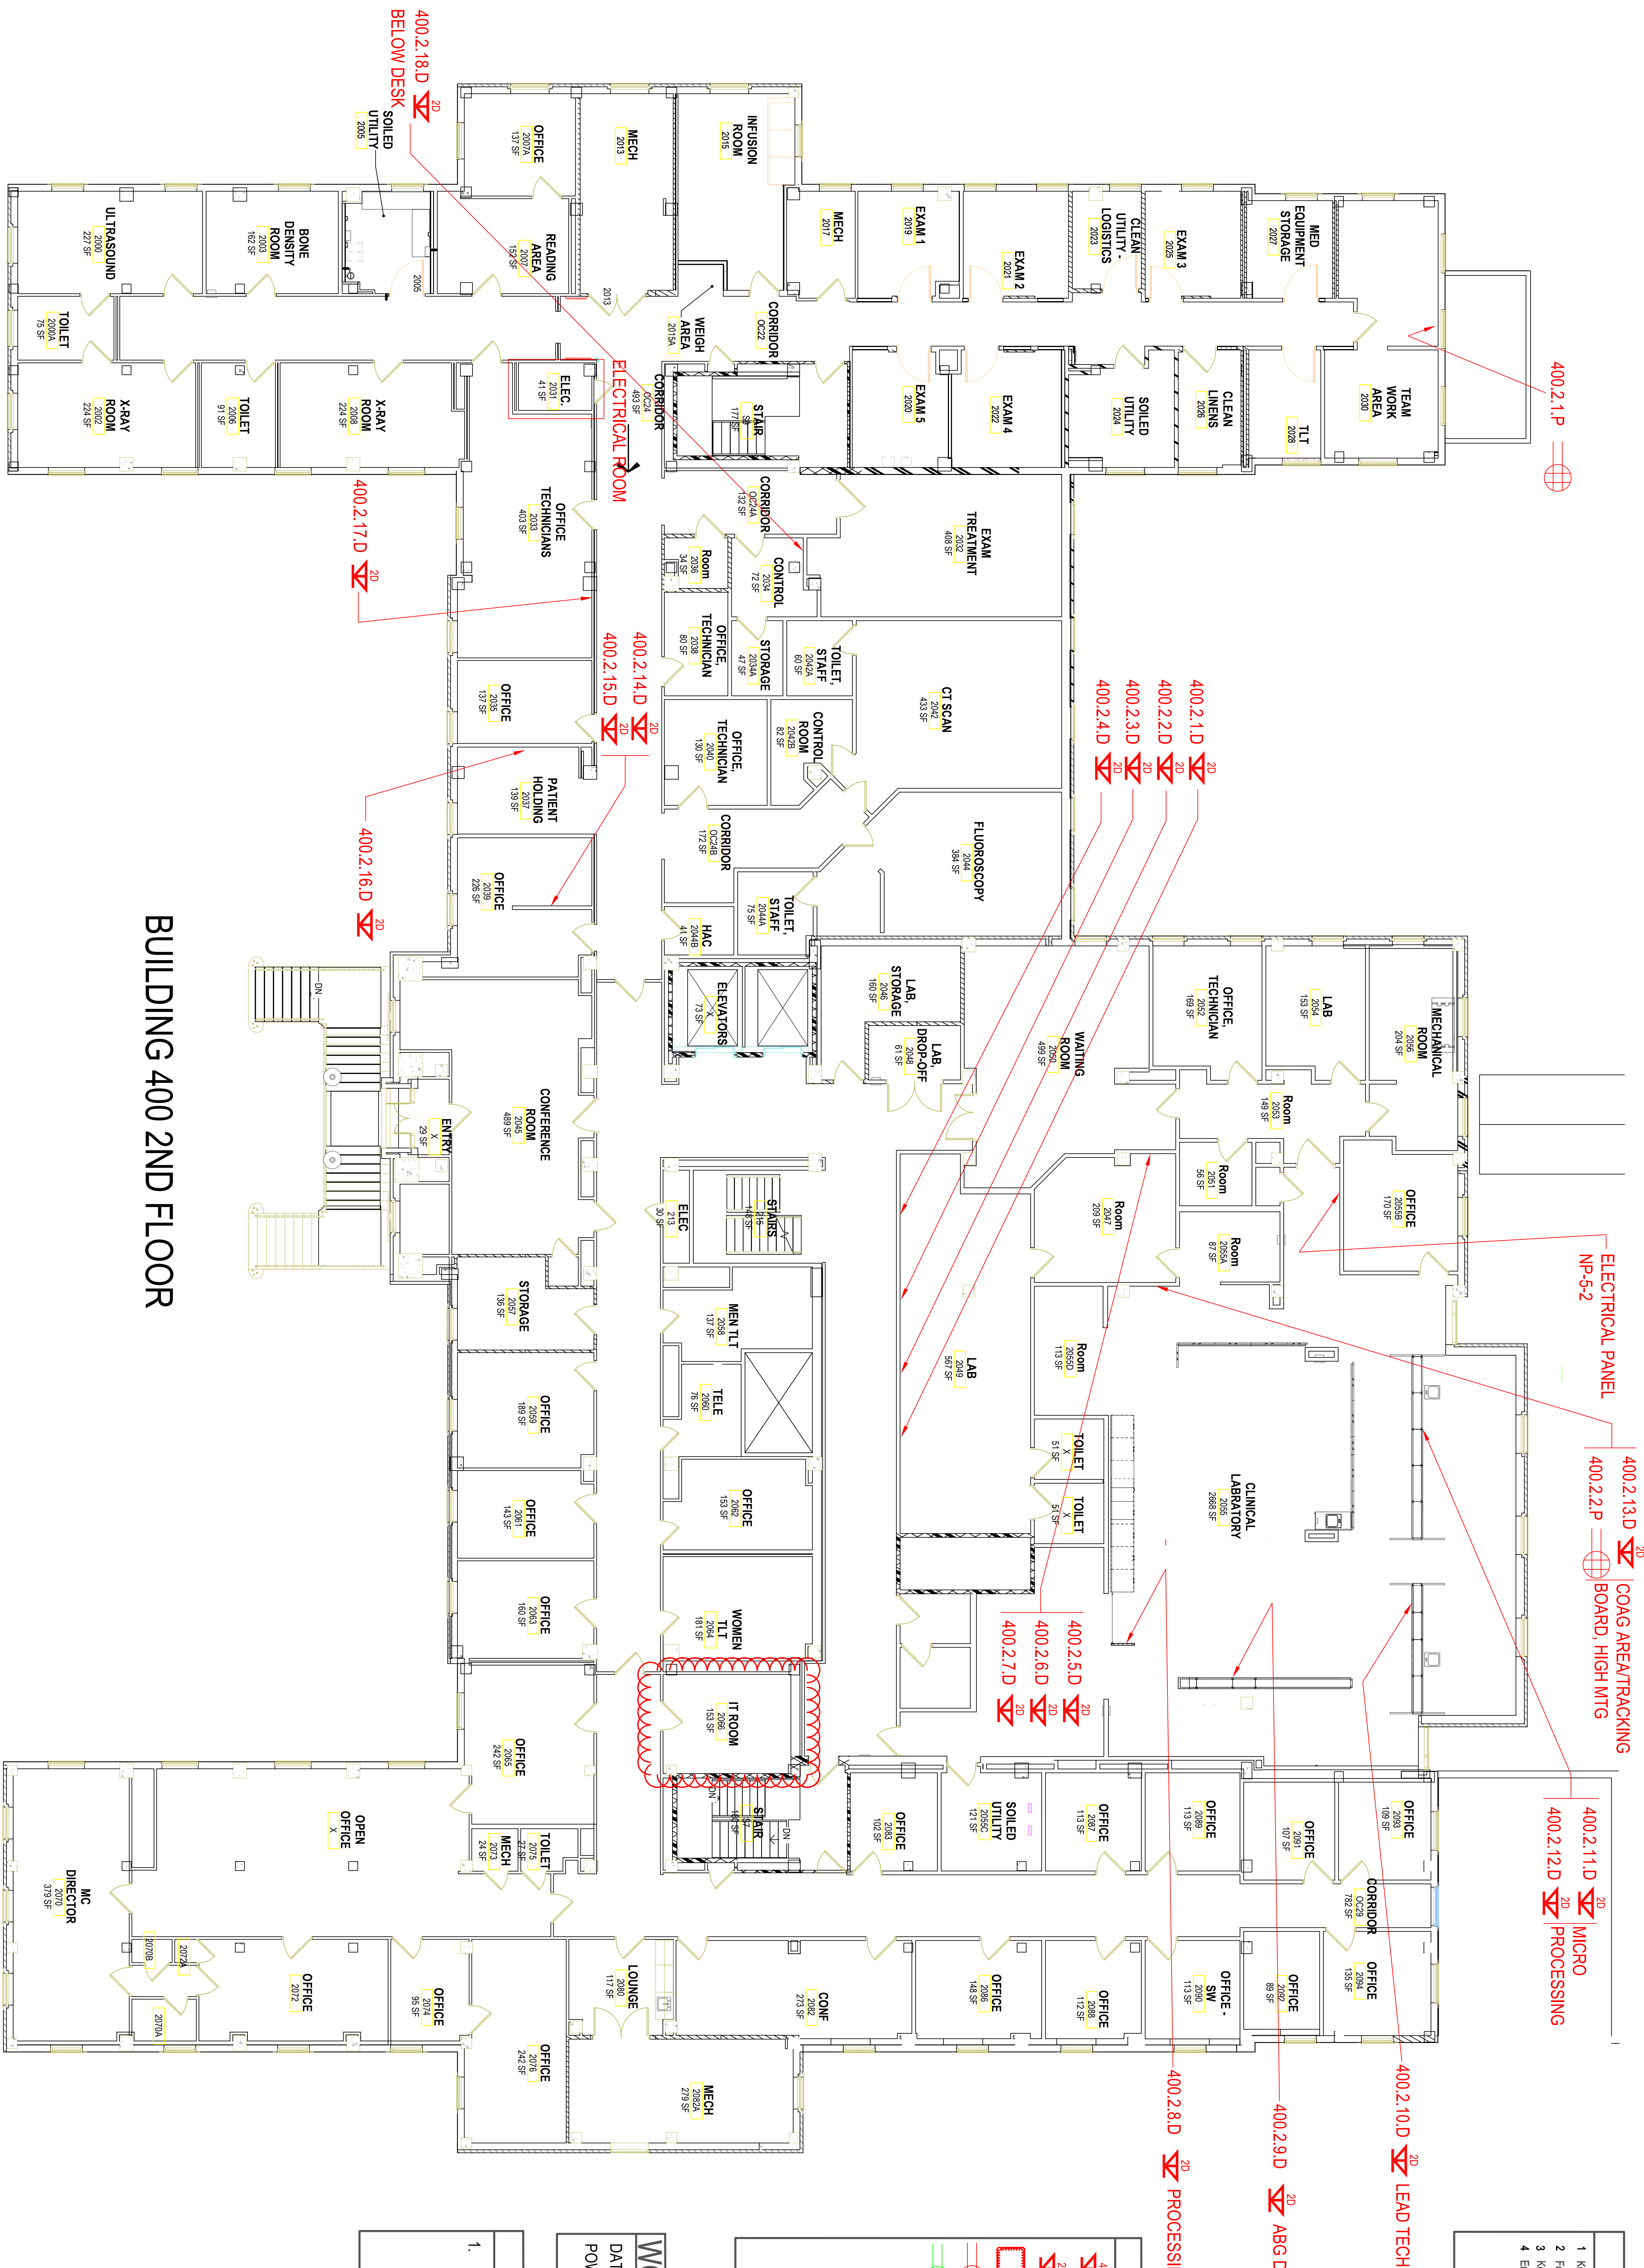


GENERAL NOTES	
1	Keep cable runs as short as possible and not to exceed 300 feet.
2	Follow ICPA requirements
3	Keep Maintenance loops as short as possible.
4	End cable with maintenance loop

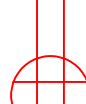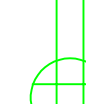REFERENCE	
	4 Port Data Outlet
	2 Port Data Outlet
	IT Closet Location
	Quadplex Outlet
	Quadplex Outlet - Emergency

WORK NEEDED	
DATA CABLE PULLS	36
POWER CABLE PULLS	2

KEY NOTE	
1.	400 2, 1, P MOUNTED HIGH, USE WALL RAIL, CIRCUIT IN PANEL NP-5-2, #33

[illegible]

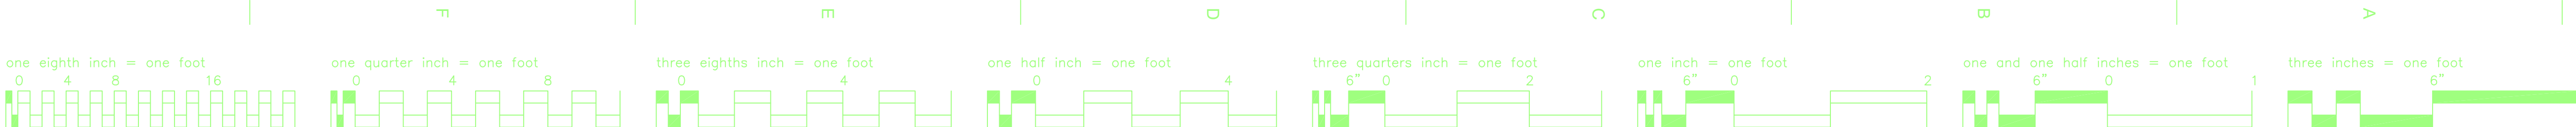

GENERAL NOTES	
1	Keep cable runs as short as possible and not to exceed 300 feet.
2	Follow ESHA requirements
3	Keep Maintenance loops as short as possible.
4	End cables with maintenance loop

REFERENCE	
	4 Port Data Outlet
	2 Port Data Outlet
	IT Closet Location
	Quadplex Outlet
	Quadplex Outlet - Emergency
	1 Port Data Outlet (1 CAT 6A CBL)

WORK NEEDED	
DATA CABLE PULLS	18
POWER CABLE PULLS	0

KEY NOTE	
1.	CONTRACTOR TO SUPPLY AND INSTALL NEW PATCH PANEL FOR DATA DROPS IN TR CLOSET. VANOSE PATCH PANEL, 48 PORT, SIMILAR TO EXISTING




4D 4 Port Data Outlet

- | | |
|---|------------------------------|
|  | 4 Port Data Outlet |
|  | 2 Port Data Outlet |
|  | IT Closet Location |
|  | Quaddplex Outlet |
|  | Quaddplex Outlet - Emergency |

DATA CABLE PULLS	4
POWER CABLE PULLS	0

1. CONTRACTOR TO SUPPLY AND INSTALL NEW PATCH PANEL FOR DATA DROPS IN TR CLOSET. V-NOSE PATCH PANEL, 48 PORT, SIMILAR TO EXISTING

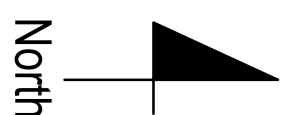

Dept. of Veterans Affairs
Medical Center
500 East Veterans Street
Tomah, WI, 54660



BLD 400 FLOOR 4

DATA DROPS POWER OUTLETS PER CSR DECEMBER 2025

Location

01-07-2026

Checked By: Drawn By

Drawn By

DDPO-400-2


Office of
Facilities
Management

GENERAL NOTES
1. Keep cable runs as short as possible and not to exceed 300 feet.
2. Follow IDCA requirements
3. Keep Maintenance loops as short as possible.
4. End cables with maintenance loop

REFERENCE
4 Port Data Outlet
2 Port Data Outlet
IT Closet Location
Quadplex Outlet
Quadplex Outlet - Emergency
Fiber Optic Cable

WORK NEEDED
DATA CABLE PULLS 4
POWER CABLE PULLS 0


KEY NOTE
1. ROUTE 402.1.1.D AND 402.1.1.D TO OLD TR CLOSET

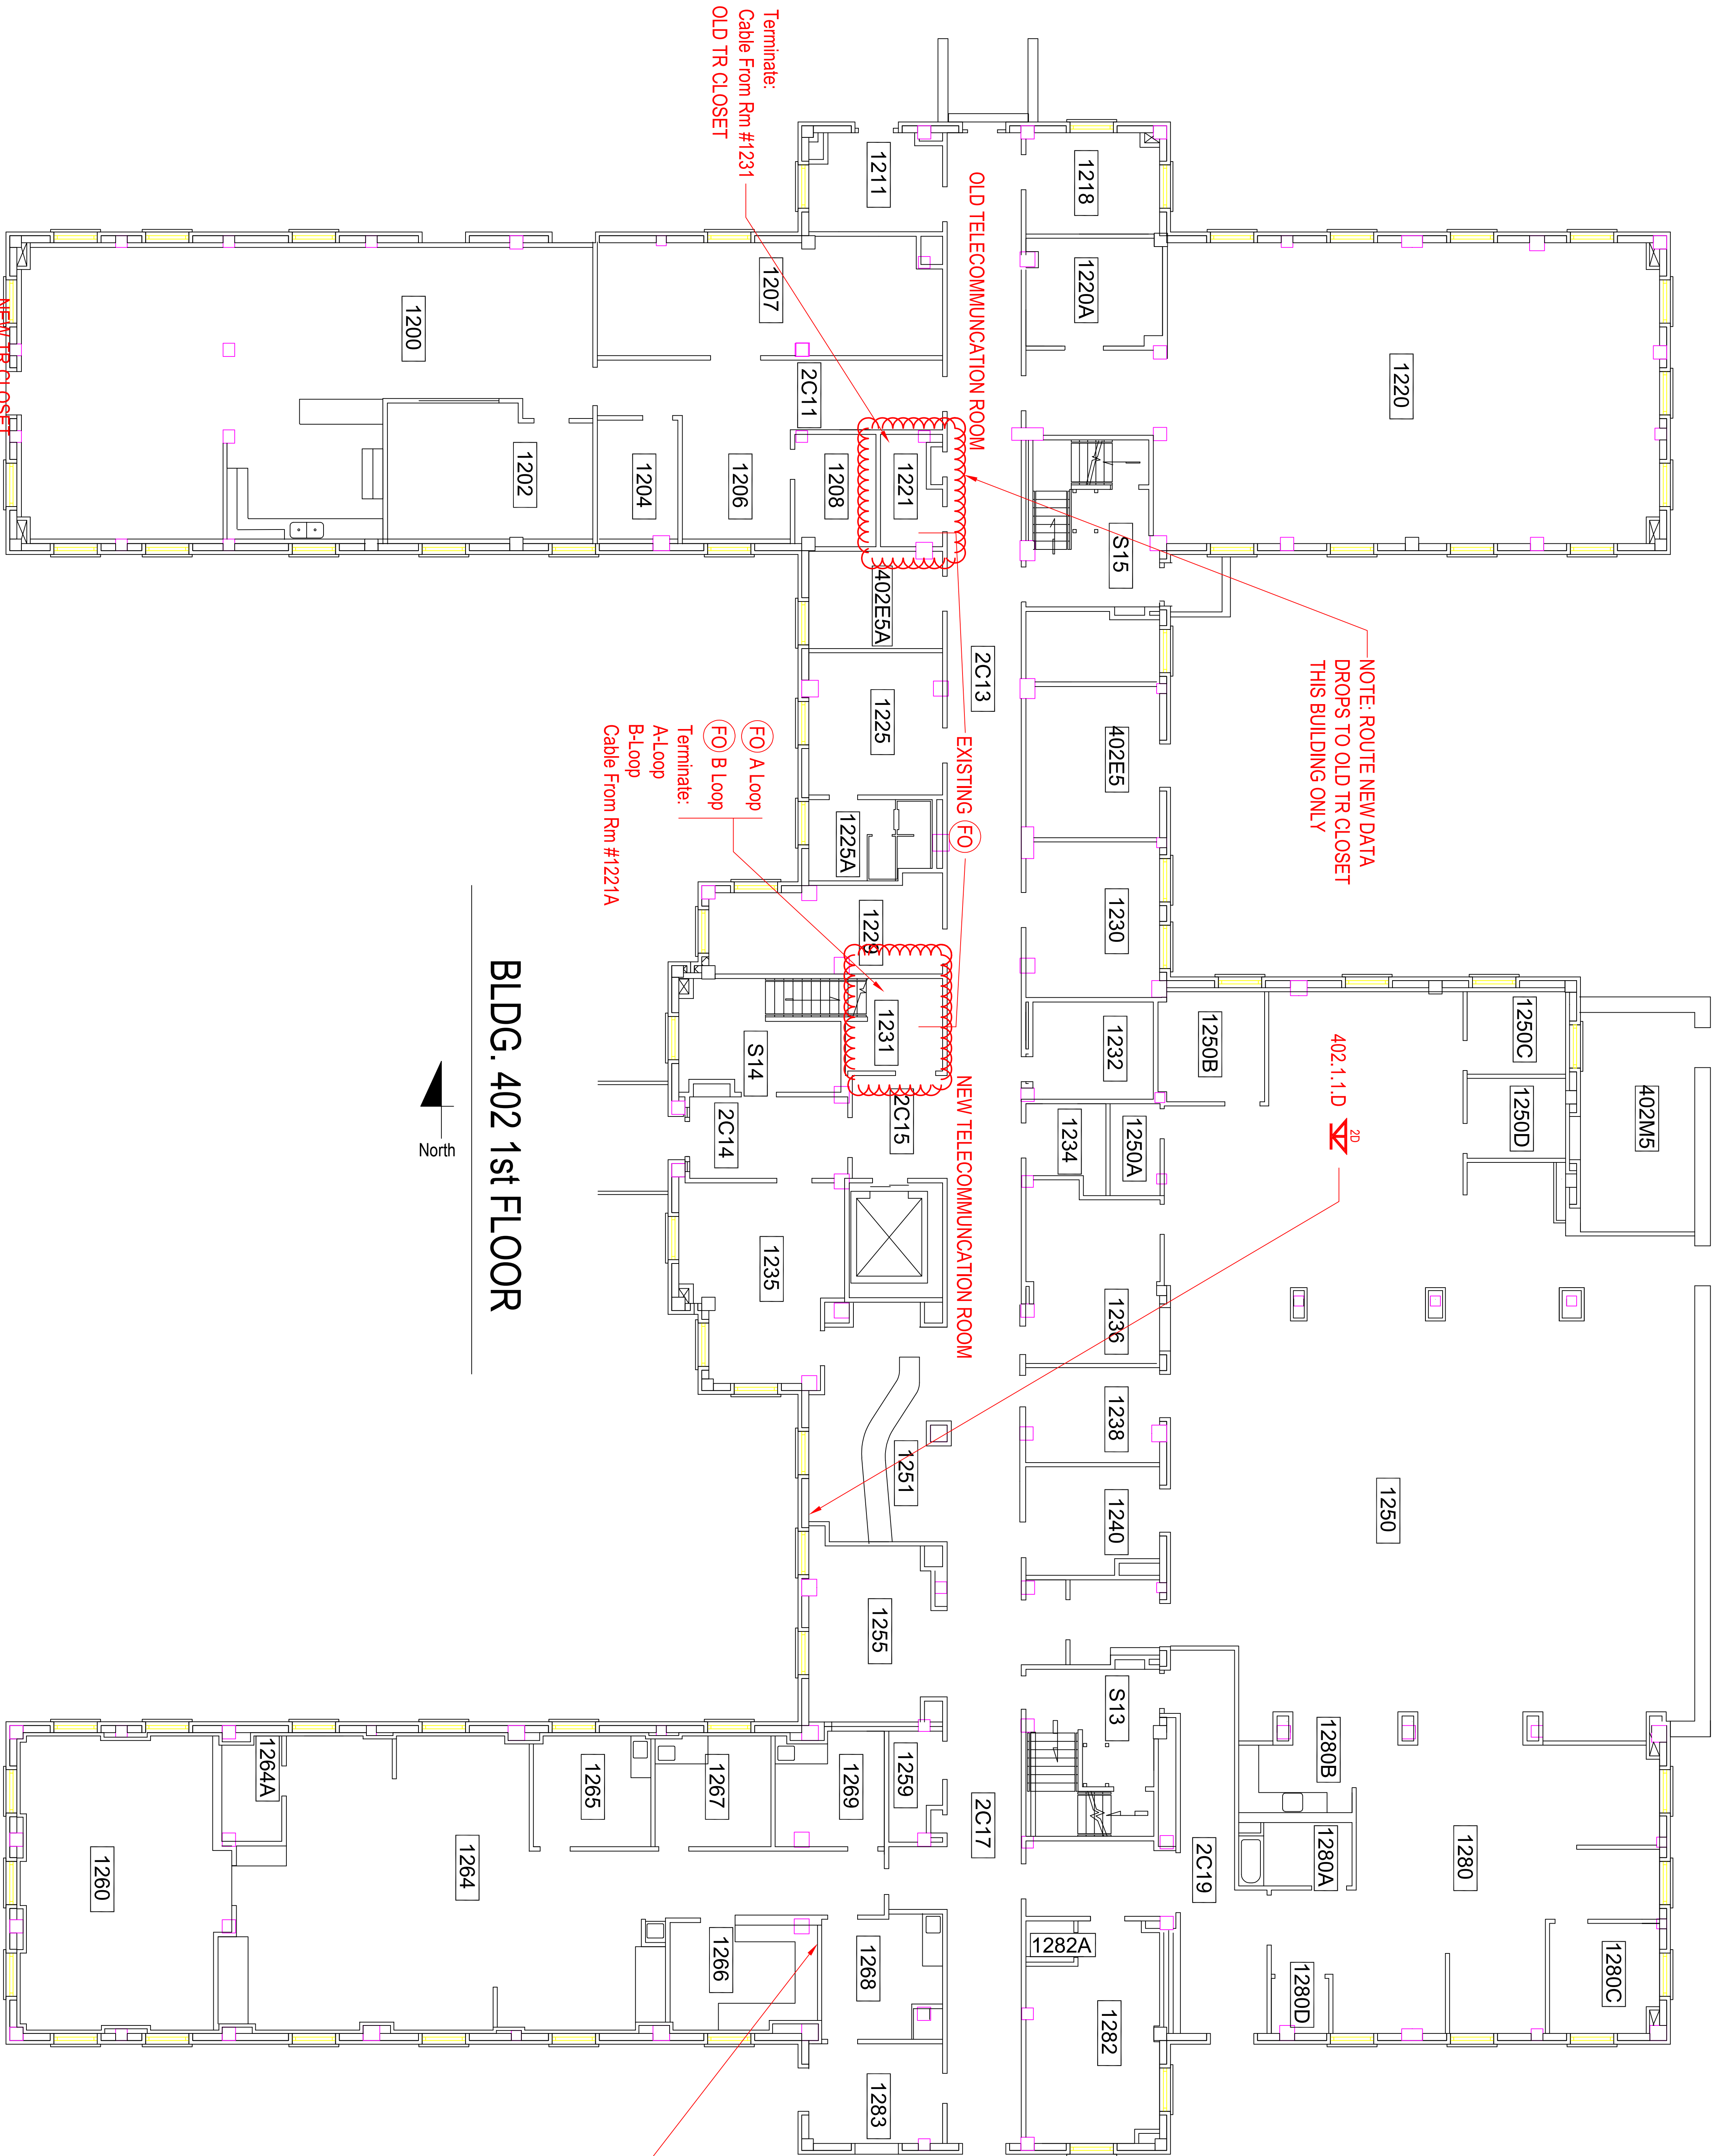

BLDG. 402 1st FLOOR



Revisions:	Date

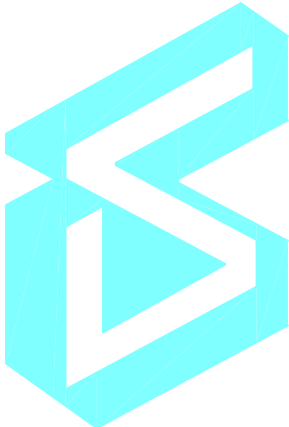

Dept. of Veterans Affairs
Medical Center
500 East Veterans Street
Tomah, WI, 54660



CONSULTANTS:

Drawing Title	Project Title
BLD 402 FLOOR 1	DATA DROPS POWER OUTLETS PER CSR DECEMBER 2025

Approved: Project Director	Location Tomah, Wisconsin
Date 01-07-2026	Checked By: JMS
	Drawn By:


Project Number 676-26-702	Building Number 400
Drawing Number DDPO-402-1	



100% - CONSTRUCTION DOCS



Office of
Facilities
Management

Department of
Veterans Affairs

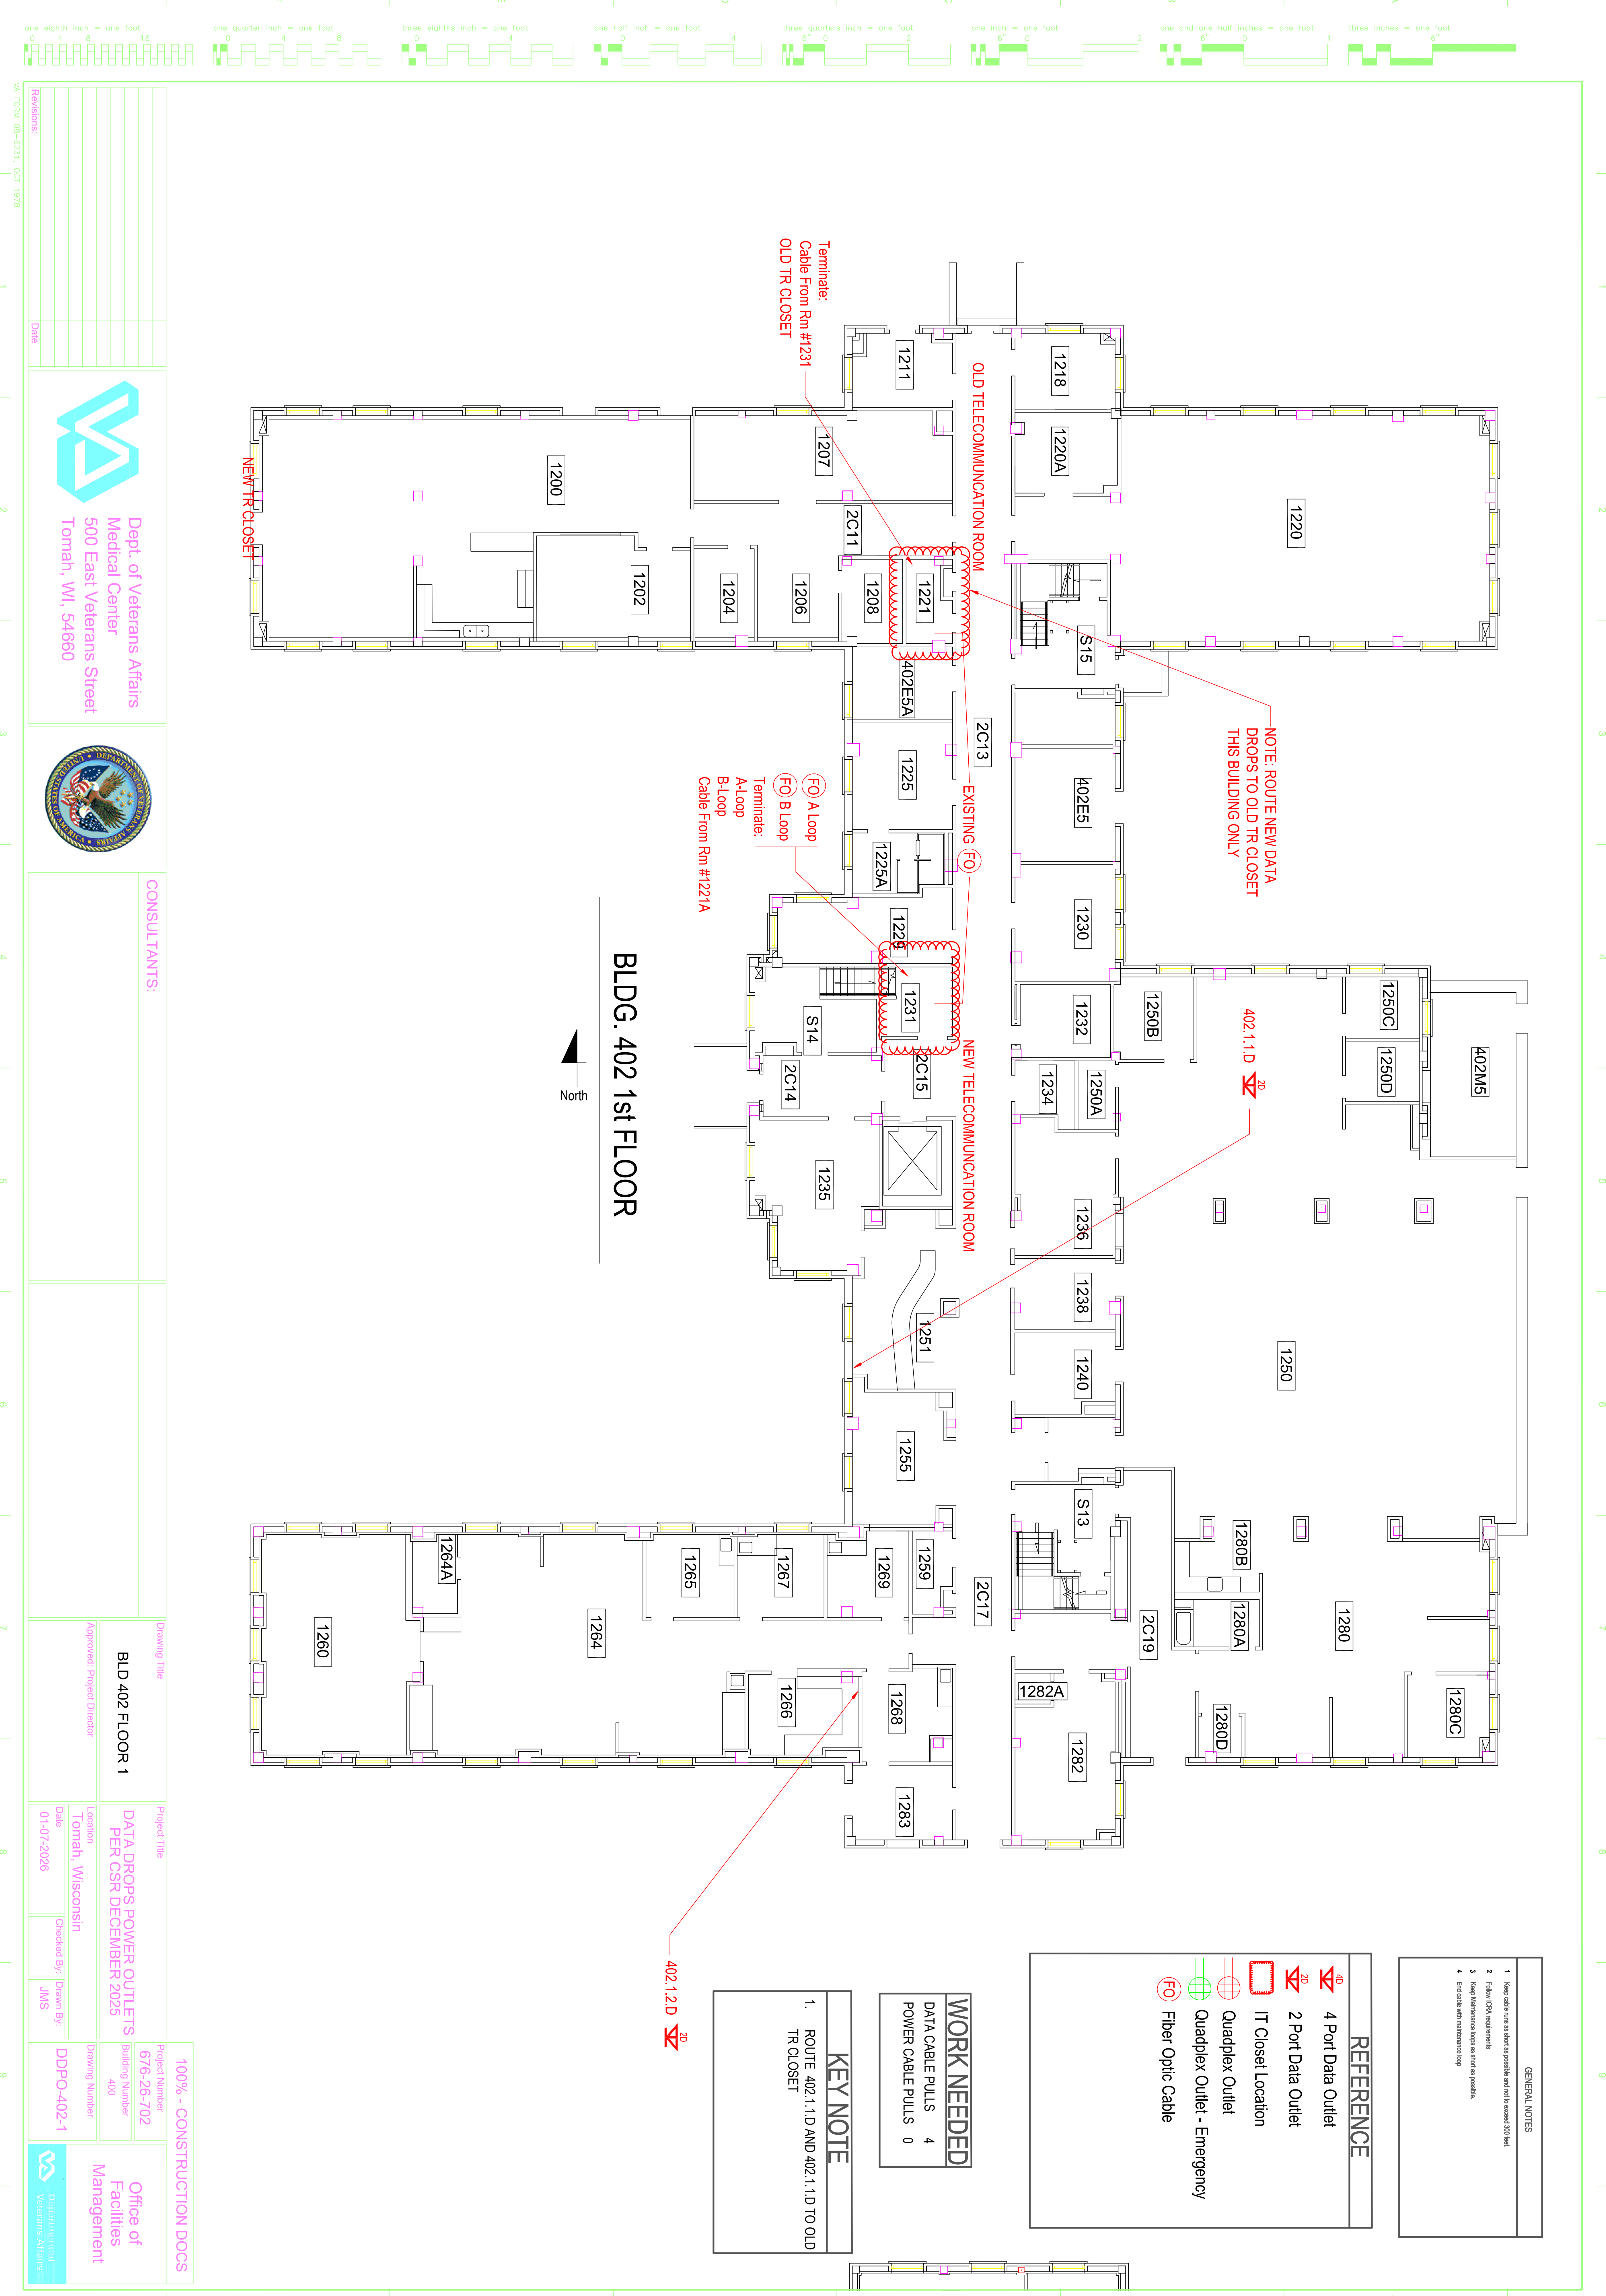

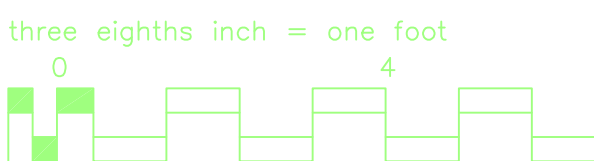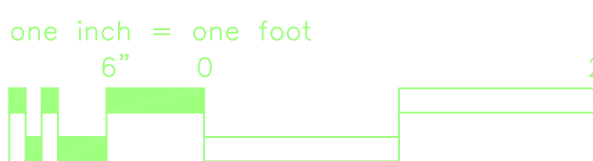



GENERAL NOTES

1. Keep cables as short as possible and not to exceed 300 feet.
2. Follow OSHA requirements
3. Keep Mastercable loop as short as possible.
4. End cables with maintenance loop

REFERENCE
 40 Port Data Outlet
 20 Port Data Outlet
 IT Closet Location
 Quadruplex Outlet
 Quadruplex Outlet - Emergency

WORK NEEDED	
DATA CABLE PULLS	2
POWER CABLE PULLS	0

KEY NOTE
1. -

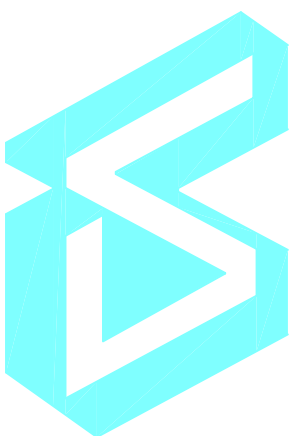
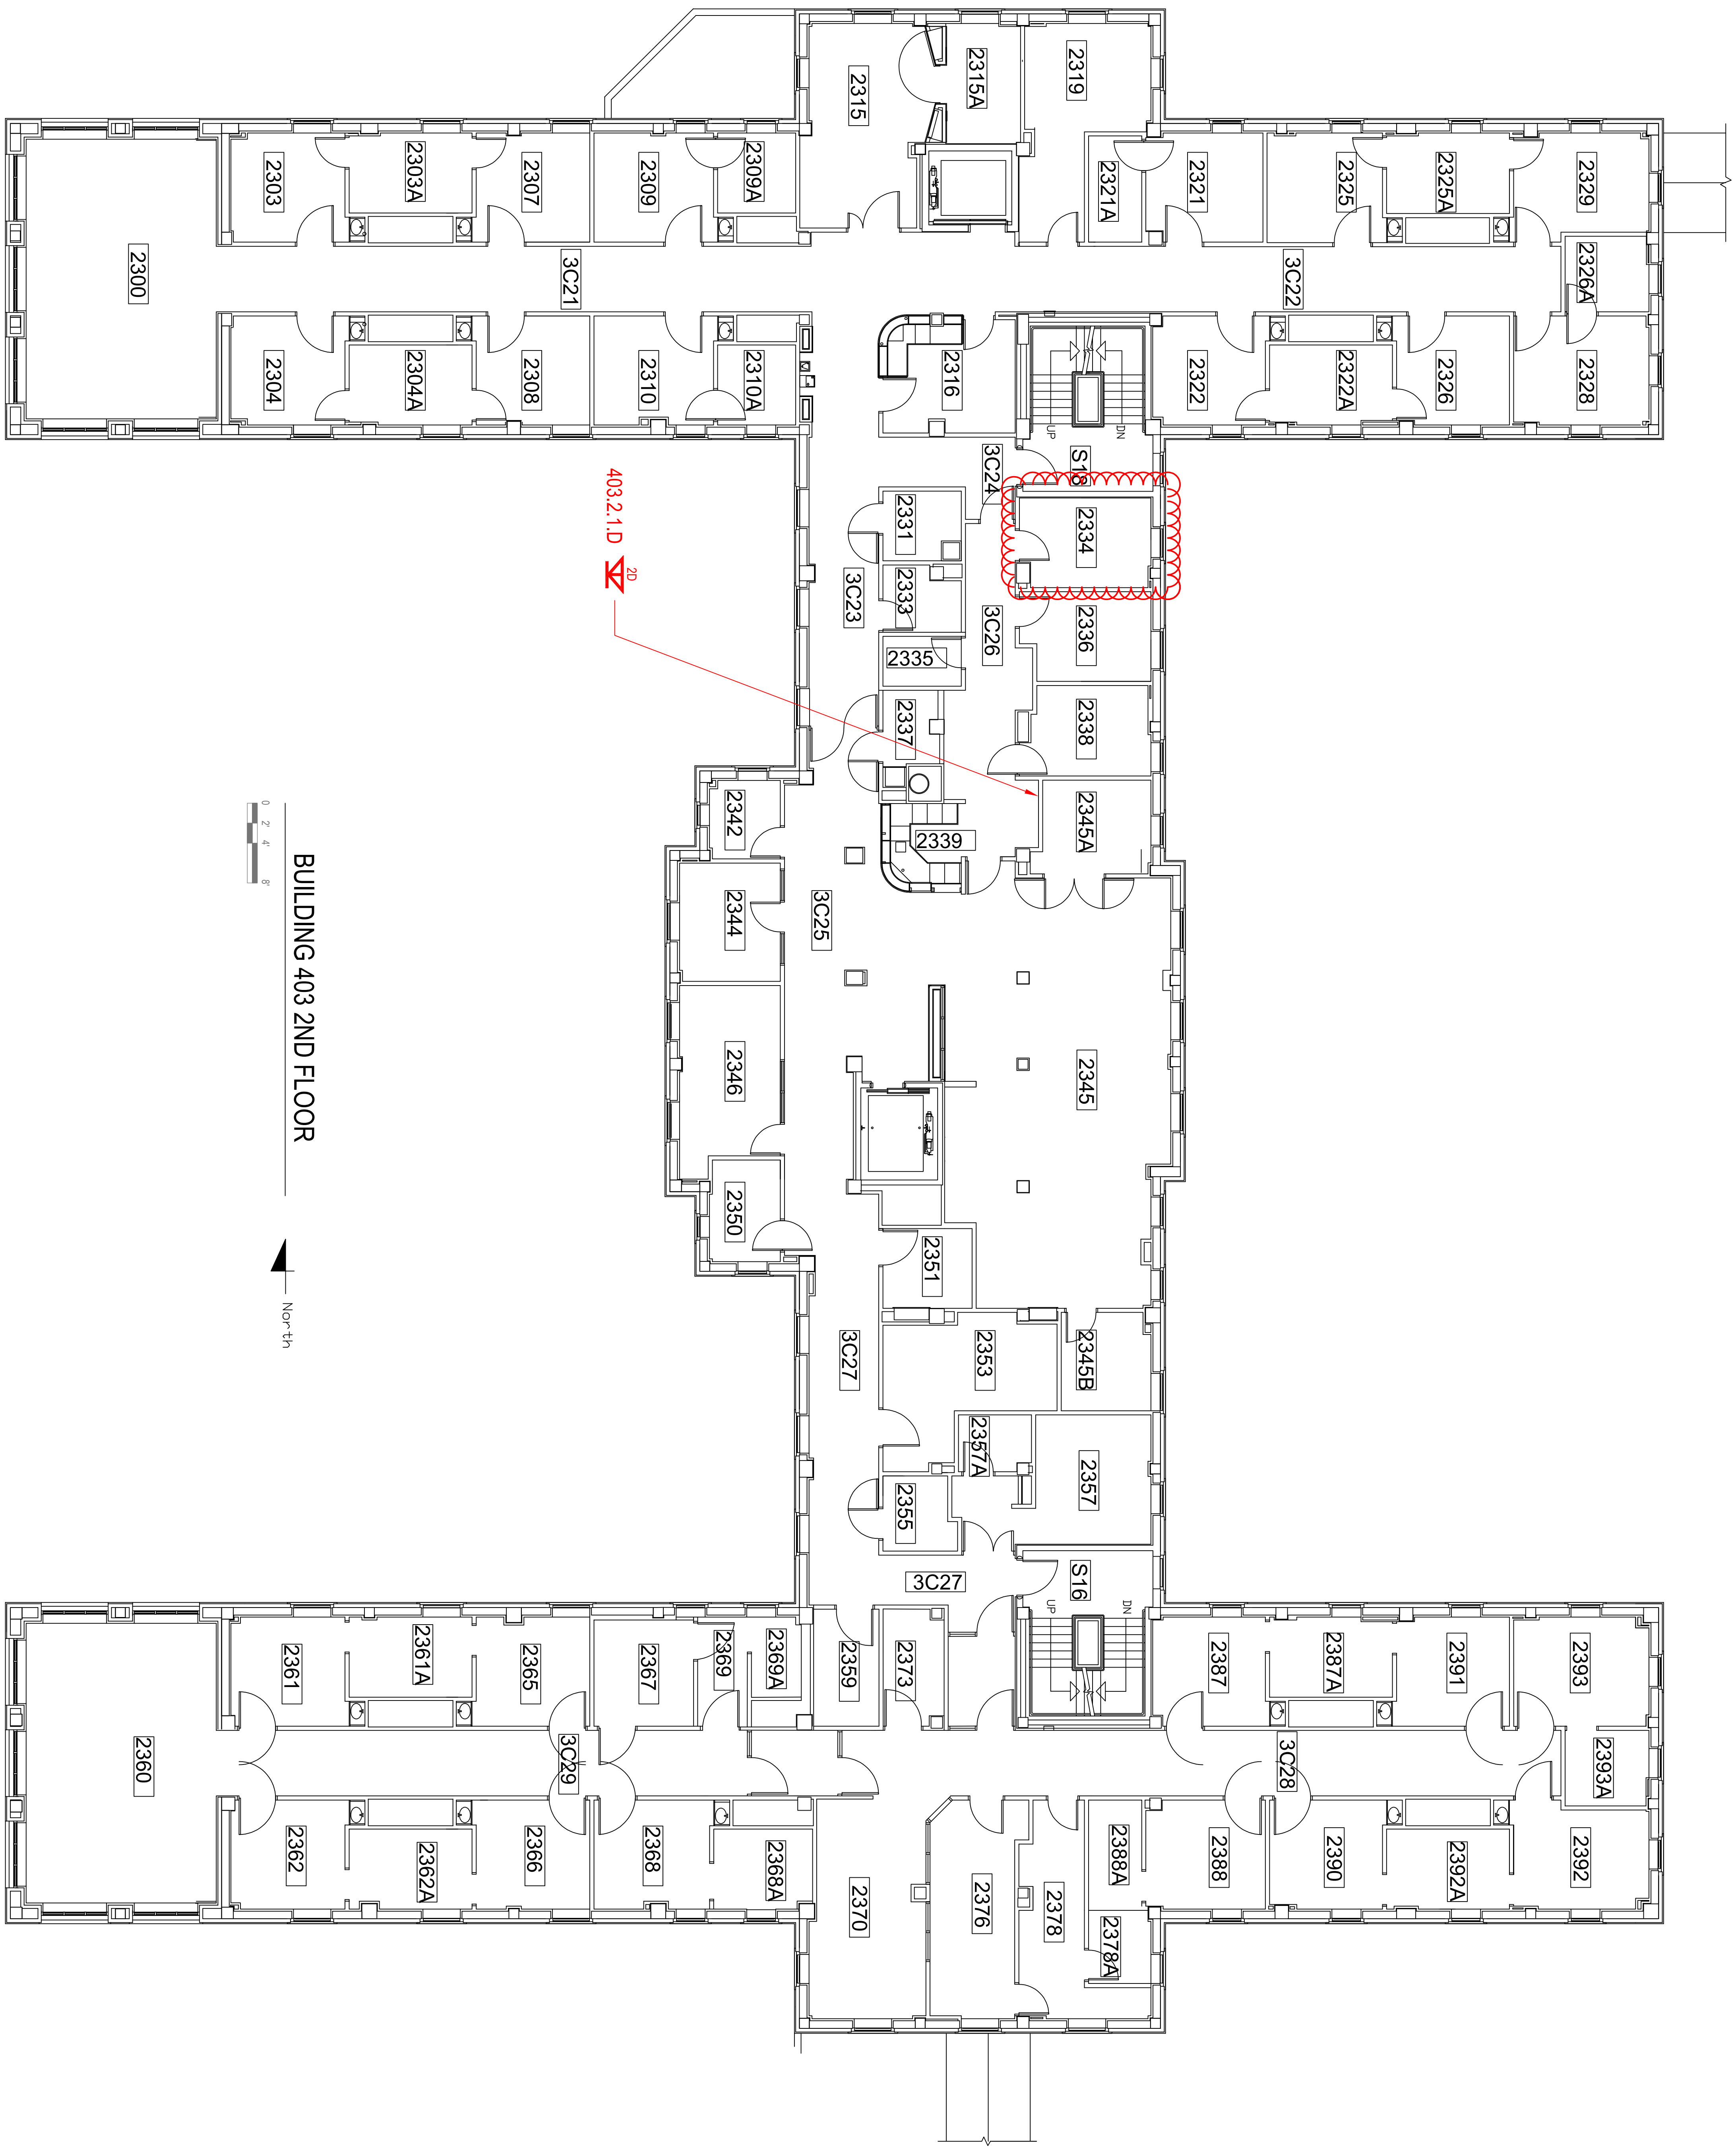


Dept. of Veterans Affairs
Medical Center
500 East Veterans Street
Tomah, WI, 54660




CONSULTANTS:

Drawing Title	Project Title			Project Number 676-26-702		Office of Facilities Management
BLD 403 FLOOR 2	DATA DROPS POWER OUTLETS PER CSR DECEMBER 2025			Building Number 400		
	Location T omah, Wisconsin			Drawing Number DDPO-403-2		
Approved: Project Director	Date 01-07-2026	Checked By	Drawn By JMS			
 Department of Valdieu Affairs						

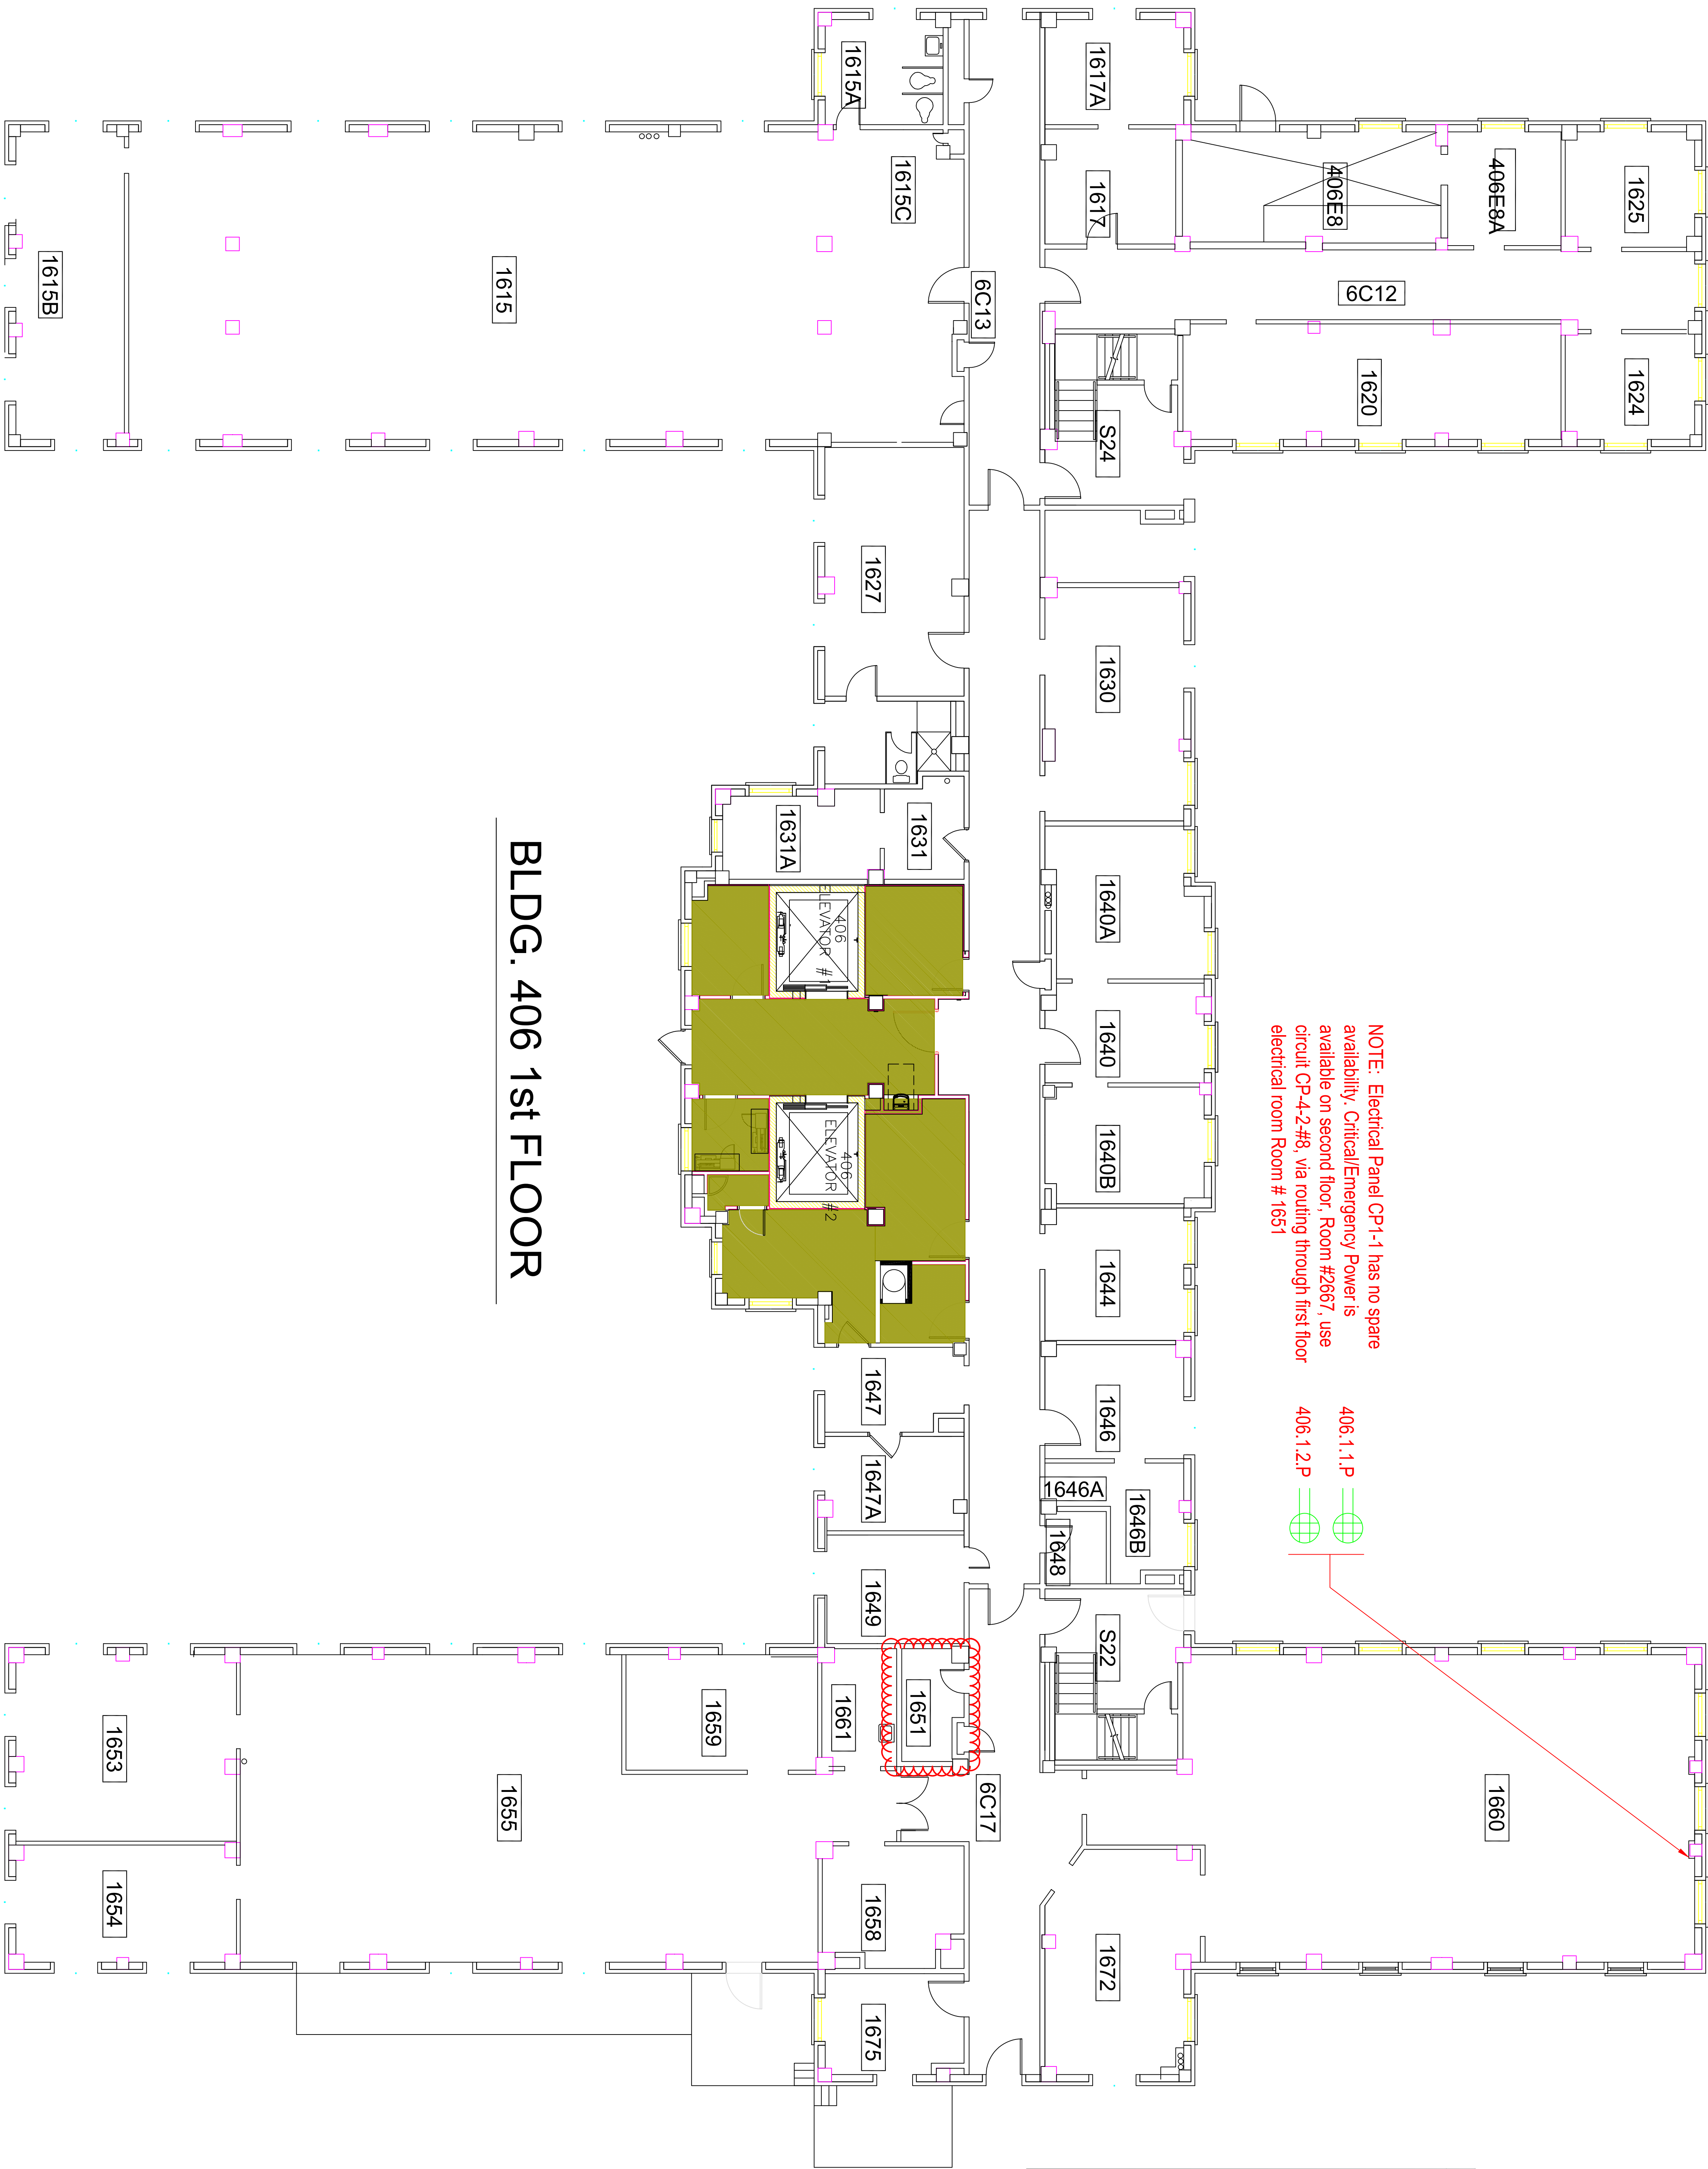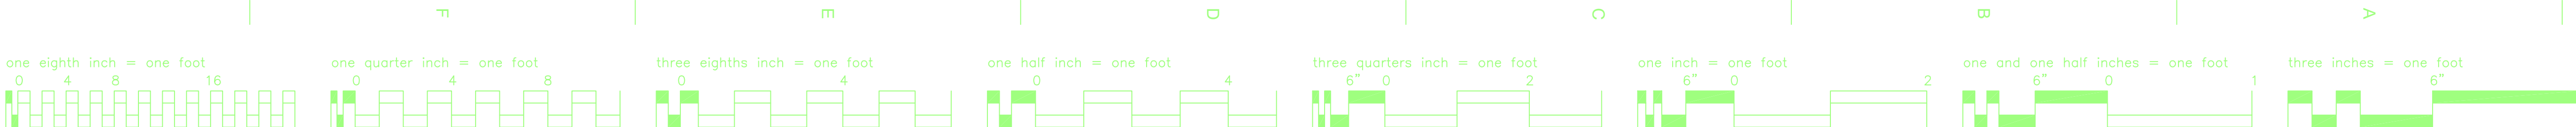

NOTE: Electrical Panel CP1-1 has no spare availability. Critical/Emergency Power is available on second floor. Room #2667, use circuit CP-4-2-#8, via routing through first floor electrical room Room # 1651

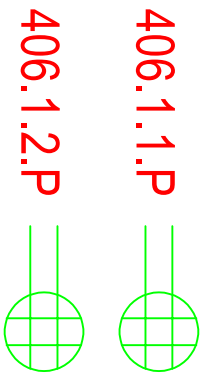

- GENERAL NOTES
- 1

Keep table tops as short as possible and not to exceed 300 feet.
- 2

Follow IDCA requirements
- 3

Keep Maintenance loops as short as possible.
- 4

End cables with maintenance loop

- REFERENCE
- 4P

4 Port Data Outlet
- 2P

2 Port Data Outlet
- IT

IT Closet Location
- Quadplex

Quadplex Outlet
- Quadplex

Quadplex Outlet - Emergency

WORK NEEDED

DATA CABLE PULLS 0

POWER CABLE PULLS 2

KEY NOTE

1. Electrical Panel CP1-1 has no spare availability. Critical/Emergency Power is available on second floor., Room #2667, use circuit CP-4-2-#8, via routing through first floor electrical room Room # 1651

BLDG. 406 1st FLOOR

Revisions:	Date

Dept. of Veterans Affairs
Medical Center
500 East Veterans Street
Tomah, WI, 54660



CONSULTANTS:	Drawing Title
	BLD 406 FLOOR 1

Project Title	Location	Date	Checked By:	Drawn By:
DATA DROPS POWER OUTLETS PER CSR DECEMBER 2025	Tomah, Wisconsin	01-07-2026	JMS	JMS

100% - CONSTRUCTION DOCS	Office of Facilities Management
Project Number 676-26-702 Building Number 400	Department of Veterans Affairs
Drawing Number DDPO-406-1	

- GENERAL NOTES
- 1

Keep cable runs as short as possible and not to exceed 300' length.
- 2

Follow OSHA requirements
- 3

Keep Maintenance loops as short as possible.
- 4

End cables with maintenance loop

REFERENCE

4D

4 Port Data Outlet

2D

2 Port Data Outlet

IT

IT Closet Location

Q

Quadplex Outlet

Q


Quadplex Outlet - Emergency

WORK NEEDED

DATA CABLE PULLS	12
POWER CABLE PULLS	0

KEY NOTE


1. -

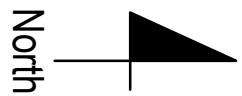

BLDG. 407 1st FLOOR

Revisions:

Date	

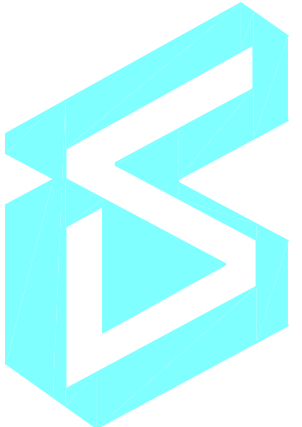

Dept. of Veterans Affairs
Medical Center
500 East Veterans Street
Tomah, WI, 54660



CONSULTANTS:

BLD 407 FLOOR 1

DATA DROPS POWER OUTLETS
PER CSR DECEMBER 2025

Location
Tomah, Wisconsin

Date
01-07-2026

Checked By:
JMS

Drawn By:
JMS


Drawing Number
DDPO-407-1

Office of
Facilities
Management
Department of
Veterans Affairs

100% - CONSTRUCTION DOCS

Project Number
676-26-702

Building Number
400

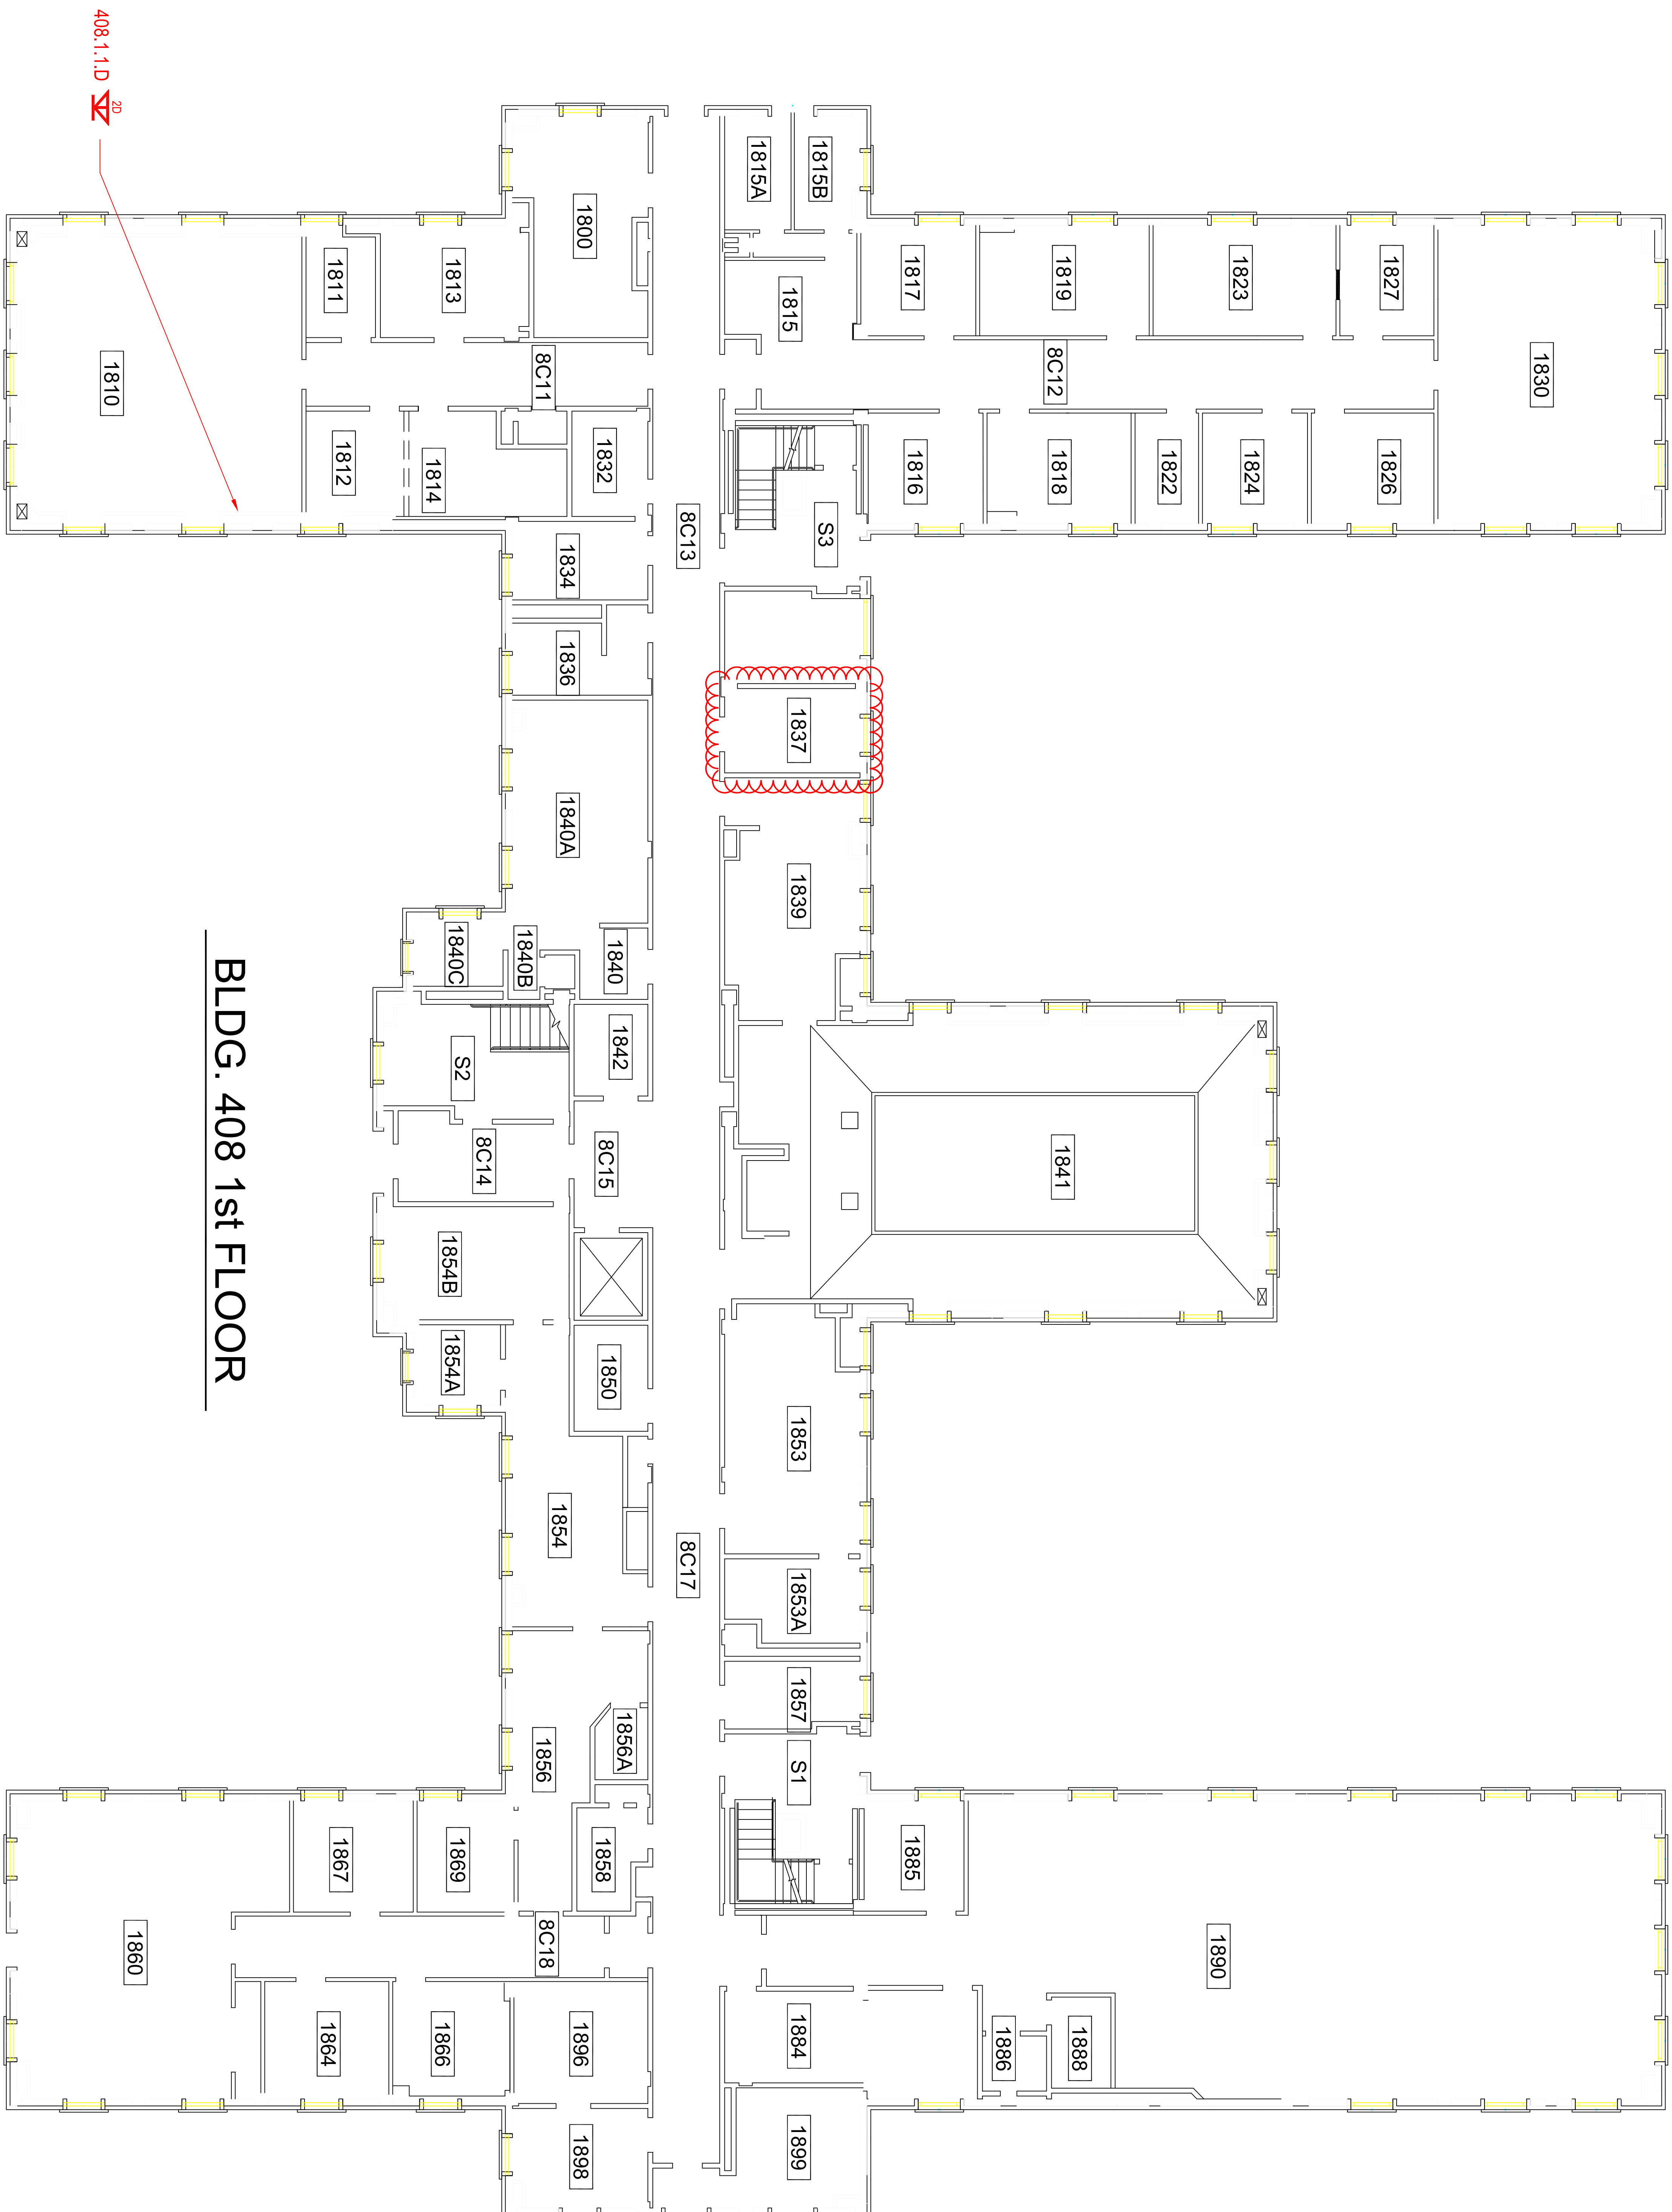


- 1 Keep dates as short as possible and do not exceed 300 beds
- 2 Follow CPGA requirements
- 3 Keep Maintenance loop as short as possible.
- 4 End dates with maintenance loop

REFERENCE
 40 Port Data Outlet
 20 Port Data Outlet
 IT Closet Location
 Quadplex Outlet
 Quadplex Outlet - Emergency

WORK NEEDED	
DATA CABLE PULLS	2
POWER CABLE PULLS	0

KEY NOTE
1. -

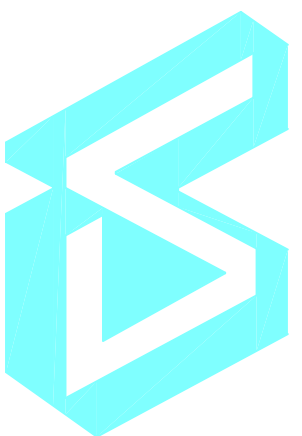

Dept. of Veterans Affairs
Medical Center
500 East Veterans Street
Tomah, WI, 54660



CONSULTANTS:

CONSULTANTS:			
Drawing Title		Project Title	
BLD 408 FLOOR 1		DATA DROPS POWER OUTLETS PER CSR DECEMBER 2025	
Approved Project Director		Location	
		Tomah, Wisconsin	
		Date	Checked By:
		01-07-2026	JMS
		Drawing Number	
		DDPO-408-1	
		Project Number	
		676-26-702	
		Building Number	
		400	
		Office of Facilities Management	
		Department of Veterans Affairs	

100% - CONSTRUCTION DOCS

Office of
Facilities
Management

Department of
Veterans Affairs

